

FOR CONSTRUCTION

LOT 2302 IN DP 1265815 LOCATED AT NO. 161 MACDONALD ROAD BARDIA NSW

PROPOSED CONSTRUCTION OF A TWO STOREY DWELLING WITH DETACHED GARAGE AND STUDIO DWELLING -LANEWAY ACCESS



BASIX™Certificate

Building Sustainability Index
www.planningportal.nsw.gov.au/development-and-assessment/basix

Multi Dwelling

Certificate number: 1821801M_03

This certificate confirms that the proposed development will meet the NSW government's requirements for sustainability, if it is built in accordance with the commitments set out below. Terms used in this certificate, or in the commitments, have the meaning given by the document entitled "BASIX Definitions" dated 10/09/2020 published by the Department. This document is available at www.planningportal.nsw.gov.au/definitions

Secretary
Date of issue: Tuesday, 11 August 2026
To be valid, this certificate must be submitted with a development application or lodged with a complying development certificate application within 3 months of the date of issue.



When submitting this BASIX certificate with a development application or complying development certificate application, it must be accompanied by NatHERS certificate 0012381470.

Project summary			
Project name	Basix-161 Macdonald Road Bardia 2565_03		
Street address	161 MACDONALD ROAD BARDIA 2565		
Local Government Area	CAMPBELLTOWN		
Plan type and plan number	Deposited Plan 1265815		
Lot No.	2302		
Section no.	-		
No. of residential flat buildings	0		
Residential flat buildings: no. of dwellings	0		
Multi-dwelling housing: no. of dwellings	2		
No. of single dwelling houses	0		
Project score			
Water	✔ 40		Target 40
Thermal Performance (Simulation method)	✔ Pass		Target Pass
Energy	✔ 73		Target 70
Materials	✔ -37		Target n/a

Unit	Description
Mn Dw	Main Dwelling
Sc Dw	Secondary Dwelling

Certificate Prepared by

Name / Company Name: SUSTAINABILITY-Z PTY LIMITED

ABN (if applicable): 59622331935

BASIX Department of Planning, Housing and Infrastructure www.basix.nsw.gov.au Version: 4.04 / EUCALYPTUS_03_01_0 Certificate No: 1821801M_03 Tuesday, 11 August 2026 page 1/21

Nationwide House Energy Rating Scheme®
Multiple Class 1 dwellings Summary
NatHERS® Certificate No. 0012381470

Generated on 11 Aug 2026 using BERS Pro v5.2.6 (3.23)

Property

Address 161 Macdonald Road,
Bardia , NSW , 2565
Lot/DP Lot 2302 DP 1265815
NatHERS Climate Zone 28 Richmond

Accredited assessor

Name Zoran Cvetkovski
Business name Sustainability-Z
Email sustainability-z@outlook.com
Phone 0414273176
Accreditation No. DMN/13/1641
Assessor Accrediting Organisation Design Matters National

Verification

To verify this certificate, scan the QR code or visit
hatar.com.au/QR/Generate?
pnVdLcshAGU
When using either link, ensure
you are visiting hatar.com.au

National Construction Code (NCC) requirements

The NCC allows the use of NatHERS accredited software to comply with the energy efficiency requirements for houses (Class 1 buildings) and apartments (Class 2 sole-occupancy units and Class 4 parts of buildings). The applicable requirements for houses are detailed in Specification 4.3 of NCC Volume Two. For apartments the requirements are detailed in clauses 3.2.3 and 3.2.15 of NCC Volume One.

The NCC, and associated ABCB Standards and support material, can be accessed at www.abcb.gov.au.
Note, variations and additions to the NCC energy efficiency requirements may apply in some states and territories.

Summary of all dwellings

Certificate number and link	Unit Number	Heating load (load limit) [MJ/m².p.a.]	Cooling load (load limit) [MJ/m².p.a.]	Total load [MJ/m².p.a.]	Star Rating	Whole of Home Rating
0012381463-02	Main Dw	36.8 (N/A)	22.9 (N/A)	59.6	7	0
0012381455-04	Sec Dw	30.1 (N/A)	29.6 (N/A)	59.7	7	0

Version 2025.0
Nationwide House Energy Rating Scheme (NatHERS) is an initiative of the Australian, state and territory governments. For more details see www.nathers.gov.au
Generated on 11 Aug 2026 using BERS Pro v5.2.6 (3.23) for 161 Macdonald Road , Bardia , NSW , 2565 Page 1 of 2

GENERAL LEGEND

AC	AIR CONDITIONING UNIT
AL	POWDERCOATED ALUMINIUM DOOR/ WINDOW
BAL	BALUSTRADE TYPE
BG	BOX GUTTER
BR1, BR2, etc.	BRICK FACE TYPE
CAP	METAL CAPPING
CD1, CD2, etc.	WALL CLADDING
CONC.	CONCRETE FLOOR
CPT	CARPET
CRT	CONCRETE ROOF TILES
CR1, CR2, etc.	CEMENT RENDER TYPE/ COLOUR
DP/S	DOWN PIPE
DW	DISH WASHER
ED	ENTRY DOOR
F	FRIDGE
FAS	FASCIA
FET	FEATURE TILE
FT, FT1, FT2, etc.	FLOOR TILES
FW	FLOOR WASTE
GD	GARAGE DOOR
GUT	GUTTER
HWU	HOT WATER UNIT
HYB	HYBRID FLOOR
L	LINEN
MR	METAL ROOF
MW	MICROWAVE OVEN
NGL	NATURAL GROUND LEVEL
OBS	OBSCURED GLASS
P	PANTRY
R	ROBE
RL	REDUCED LEVEL
RWH	RAIN WATER HEAD
RWT	RAIN WATER TANK
S	STORAGE
TOW	TOP OF WALL
TL	TIMBER LAMINATE
WC	WATER CLOSET
WM	WASHING MACHINE
SD	SMOKE DETECTOR

Sheet List 2		
Sheet Number	Sheet Name	Drawn By
CC.01	COVER SHEET	rohit
CC.02A	GENERAL NOTES A	rohit
CC.02B	GENERAL NOTES B	rohit
CC.03	LOCATION PLAN AND SITE PLAN	rohit
CC.04	SITE ANALYSIS AND SEDIMENT CONTROL	rohit
CC.05	GROUND FLOOR PLAN	rohit
CC.06	FIRST FLOOR LEVEL	rohit
CC.07	ROOF PLAN	rohit
CC.08	ELEVATION 01	rohit

Sheet List 2		
Sheet Number	Sheet Name	Drawn By
CC.09	ELEVATION 02	rohit
CC.10	SECTIONS	rohit
CC.11	AREA PLAN CALCULATION	rohit
CC.12	ROOM AREA PLAN	rohit
CC.13	COLOR SCHEDULE	rohit
CC.14	LANDSCAPE PLAN	rohit
CC.15	BASIX	rohit
CC.15a	BASIX 01	rohit
CC.18	DOOR/ WINDOW SCHEDULE	rohit
CC.19	DRIVEWAY DETAILS	rohit

CC ISSUE

REV	DATE	DESCRIPTION	BY
2	24-07-2026	DA MOD	
1	03-02-2026	DA ISSUE	



THIS DRAWING IS THE EXCLUSIVE PROPERTY OF THE DEVELOPER & THE REPRODUCTION OF ANY PART WITHOUT THE PRIOR WRITTEN CONSENT OF THE DEVELOPER IS A VIOLATION OF APPLICABLE LAWS. IN NO EVENT SHALL THE DEVELOPER BE HELD LIABLE FOR SPECIAL COLLATERAL, INCIDENTAL OR CONSEQUENTIAL LIABILITY IN CONNECTION WITH THE USE OF THIS DIGITAL DATA ONCE RELEASED FROM THE DEVELOPER'S OFFICE. THIS DRAWING IS TO BE READ & UNDERSTOOD IN CONJUNCTION WITH THE STRUCTURAL, MECHANICAL, ELECTRICAL & / OR ANY OTHER CONSULTANT'S DOCUMENTATION AS MAY BE APPLICABLE TO THE PROJECT PRIOR TO THE START OF ANY WORKS AND FOR ITS DURATION.

PROJECT:

LOT 2302 IN DP 1265815

161 MacDonald Rd
Bardia NSW

DRAWING TITLE:

COVER SHEET

NORTH:

LOT NO:

2302

DRAWN BY:

ROHIT
rohit

DATE:

1-10-2026

CHECKED BY:

RH

SCALE:

1 : 100

DRAWING No:

CC.01

REV:

2
ISSUED BY:

CLIENT NAME:

Yuliana Chongbang

BUILDING SPECIFICATIONS

National Construction Code – Volume 2, Amendment 1 – Building Code of Australia 2022 & Housing Provisions Standard 2022

SITE PREPARATION

- PART 3.1 OF THE NCC VOLUME 2, AMENDMENT 1 - BUILDING CODE OF AUSTRALIA 2022 & HOUSING PROVISIONS STANDARD 2022.

EARTHWORKS

- TO BE CARRIED OUT IN ACCORDANCE WITH THE REQUIREMENTS OF THE ENVIRONMENTAL PLANNING & ASSESSMENT ACT 1979 AND DEVELOPMENT CONSENT CONDITIONS
- PART 3.2 OF THE NCC VOLUME 2, AMENDMENT 1 - BUILDING CODE OF AUSTRALIA 2022 & HOUSING PROVISIONS STANDARD 2022.
- AS 4678:2002 - EARTH-RETAINING STRUCTURES

DRAINAGE

- PART 3.3 OF THE NCC VOLUME 2, AMENDMENT 1 - BUILDING CODE OF AUSTRALIA 2022 & HOUSING PROVISIONS STANDARD 2022.
- AS/NZS 3500.1:2021 - PLUMBING & DRAINAGE - WATER SERVICES
- AS/NZS 3500.2:2021 - PLUMBING & DRAINAGE - SANITARY PLUMBING & DRAINAGE
- AS/NZS 3500.3:2021 - PLUMBING & DRAINAGE STORMWATER DRAINAGE
- AS/NZS 3500.4:2021 - PLUMBING & DRAINAGE - HEATED WATER SERVICES

STRUCTURAL WORK

- Part 2.2 OF THE NCC VOLUME 2, AMENDMENT 1 - BUILDING CODE OF AUSTRALIA 2022 & HOUSING PROVISIONS STANDARD 2022.
- AS 4100:2020 - STEEL STRUCTURES CODES
- AS/NZS 1170.0:2002 - GENERAL PRINCIPLES
- AS/NZS 1170.1:2002 - PARTS 1 PERMANENT, IMPOSED AND OTHER ACTIONS
- AS/NZS 1170.2:2021 - PART 2 WIND ACTIONS
- AS 3700:2018 - SAA MASONRY CODE
- AS 1684.3:2021 - RESIDENTIAL TIMBER FRAMED CONSTRUCTION

FOOTINGS & SLABS

- PART 4 OF THE NCC VOLUME 2, AMENDMENT 1 - BUILDING CODE OF AUSTRALIA 2022 & HOUSING PROVISIONS STANDARD 2022.
- AS 2159:2009 - PILING - DESIGN & INSTALLATION
- AS 2870:2011 - RESIDENTIAL SLABS & FOOTINGS
- AS 3600:2018 - CONCRETE STRUCTURES

MASONRY

- PART 5 OF THE NCC VOLUME 2, AMENDMENT 1 - BUILDING CODE OF AUSTRALIA 2022 & HOUSING PROVISIONS STANDARD 2022.
- AS 3700:2018 - MASONRY STRUCTURES

FRAMING

- PART 6 OF THE NCC VOLUME 2, AMENDMENT 1 - BUILDING CODE OF AUSTRALIA 2022 & HOUSING PROVISIONS STANDARD 2022.
- AS 1684.2:2021 - RESIDENTIAL TIMBER-FRAMED CONSTRUCTION - NON- CYCLONIC AREAS
- AS 1720.1:2010 - TIMBER STRUCTURES - DESIGN METHODS
- AS 4100:2020 - STEEL STRUCTURES
- AS 3660.1:2014 - TERMITE MANAGEMENT SYSTEM

ROOF & WALL CLADDING

- PART 7 OF THE NCC VOLUME 2, AMENDMENT 1 - BUILDING CODE OF AUSTRALIA 2022 & HOUSING PROVISIONS STANDARD 2022.
- AS 1273:1991 - UNPLASTICIZED PVC (UPVC) DOWNPIPES & FITTINGS FOR RAINWATER
- AS 1562.1:2018 - DESIGN & INSTALLATION OF SHEET ROOF & WALL CLADDING - METAL
- AS/NZS 1562.3:2006 - DESIGN & INSTALLATION OF SHEET ROOF & WALL CLADDING - PLASTIC
- AS 2049:2002 - ROOF TILES
- AS 2050:2018 - INSTALLATION OF ROOF TILES
- AS 4285:2019 - ROOFLIGHTS

GLAZING

- PART 8 OF THE NCC VOLUME 2, AMENDMENT 1 - BUILDING CODE OF AUSTRALIA 2022 & HOUSING PROVISIONS STANDARD 2022.
- AS 1288:2021 - GLASS IN BUILDINGS - SELECTION & INSTALLATION
- AS 2047:2014 - WINDOWS & EXTERNAL GLAZED DOORS IN BUILDINGS
- AS/NZS 2208:1996 - SAFETY GLAZING MATERIALS IN BUILDINGS

FIRE SAFETY

- PART 9 OF THE NCC VOLUME 2, AMENDMENT 1 - BUILDING CODE OF AUSTRALIA 2022 & HOUSING PROVISIONS STANDARD 2022.
- AS 3786:2014 - SMOKE ALARMS USING SCATTERED LIGHT, TRANSMITTED LIGHT OR IONIZATION

HEALTH & AMENITY

- PART 10 OF THE NCC VOLUME 2, AMENDMENT 1 - BUILDING CODE OF AUSTRALIA 2022 & HOUSING PROVISIONS STANDARD 2022.
- AS/NZS ISO 717.1:2004 - ACOUSTICS - RATING OF SOUND INSULATION IN BUILDINGS & OF BUILDING ELEMENTS - AIRBORNE SOUND INSULATION
- AS ISO 717.2:2004 - ACOUSTICS - RATING OF SOUND INSULATION IN BUILDINGS & OF BUILDING ELEMENTS - IMPACT SOUND INSULATION
- AS 1668.2:2012 - THE USE OF VENTILATION & AIR CONDITIONING IN BUILDINGS - MECHANICAL VENTILATION IN BUILDINGS
- AS 1668.4:2012 - THE USE OF VENTILATION & AIR CONDITIONING IN BUILDINGS - NATURAL VENTILATION OF BUILDINGS
- AS/NZS 1680.0:2009 - INTERIOR LIGHTING - SAFE MOVEMENT
- AS 3740:2021 - WATERPROOFING OF DOMESTIC WET AREAS
- AS 3000:2018 - ELECTRICAL INSTALLATION
- BCA Part 10.8.1, AS4200.1 & AS4200.2 - PLIABLE BUILDING MEMBRANE INSTALLED.

WATERPROOFING

- PART 10.2 OF THE NCC VOLUME 2, AMENDMENT 1 - BUILDING CODE OF AUSTRALIA 2022 & HOUSING PROVISIONS STANDARD 2022
- AS 3740:2021 - WATERPROOFING TO WET AREA
- AS 4654:2012 - EXTERNAL WET AREAS

SAFE MOVEMENT & ACCESS

- PART 11 OF THE NCC VOLUME 2, AMENDMENT 1 - BUILDING CODE OF AUSTRALIA 2022 & HOUSING PROVISIONS STANDARD 2022.
- AS 1428.1:2009 - DESIGN FOR ACCESS & MOBILITY - GENERAL REQUIREMENTS FOR ACCESS - NEW BUILDING WORK
- AS 1657:2018 - FIXED PLATFORMS, WALKWAYS, STAIRWAYS & LADDERS - DESIGN, CONSTRUCTION & INSTALLATION

HANDRAILS & BALUSTRADE

- PART 11.3.3 OF THE NCC VOLUME 2, AMENDMENT 1 - BUILDING CODE OF AUSTRALIA 2022 & HOUSING PROVISIONS STANDARD 2022.
- PART 11.3.4 OF THE NCC VOLUME 2, AMENDMENT 1 - BUILDING CODE OF AUSTRALIA 2022 & HOUSING PROVISIONS STANDARD 2022.
- PART 11.3.5 OF THE NCC VOLUME 2, AMENDMENT 1 - BUILDING CODE OF AUSTRALIA 2022 & HOUSING PROVISIONS STANDARD 2022.
- AS 1170.1:2002 - BALUSTRADE INSTALLATION

PROTECTION OF OPENABLE WINDOW


PART 11.3.7 AND 11.3.8 OF THE NCC VOLUME 2, AMENDMENT 1 - BUILDING CODE OF AUSTRALIA 2022 & HOUSING PROVISIONS STANDARD 2022.

ENERGY EFFICIENCY


- PART 13 OF THE NCC VOLUME 2, AMENDMENT 1 - BUILDING CODE OF AUSTRALIA 2022 & HOUSING PROVISIONS STANDARD 2022 & BASIX CERTIFICATE.

MECHANICAL VENTILATION

- EXHAUST FROM A BATHROOM, SANITARY COMPARTMENT TO DISCHARGE DIRECTLY TO OUTDOOR AIR WITH MINIMUM FLOW RATE OF 25L/S & MAKE-UP AIR VIA OPENINGS TO AN ADJACENT ROOM WITH A FREE AREA OF 14,000 MM². THIS EXHAUST SYSTEM MUST BE INTERLOCKED WITH LIGHT SWITCH AND INCLUDE RUN-ON TIMER SO THAT THE EXHAUST SYSTEM CONTINUES TO OPERATE FOR 10 MINUTES AFTER THE LIGHT SWITCH IS OFF.
- ANY INSTALLED - KITCHEN RANGEHOOD EXHAUST TO DISCHARGE DIRECTLY OR VIA DUCT TO OUTDOOR AIR WITH MINIMUM FLOW RATE OF 40L/S & MAKE-UP AIR VIA OPENINGS TO AN ADJACENT ROOM WITH A FREE AREA OF 14,000 MM².
- LAUNDRY EXHAUST TO DISCHARGE DIRECTLY OR VIA DUCT TO OUTDOOR AIR WITH MINIMUM FLOW RATE OF 40L/S & MAKE-UP AIR VIA OPENINGS TO AN ADJACENT ROOM WITH A FREE AREA OF 14,000 MM².

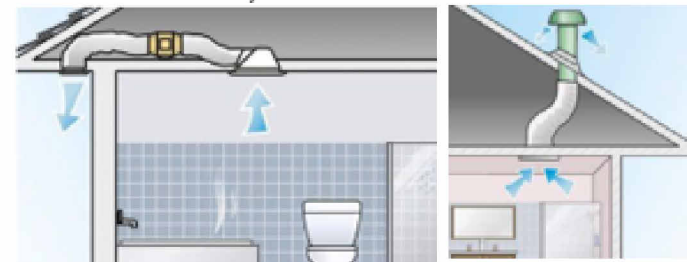

REV	DATE	DESCRIPTION	BY
2	24-07-2026	DA MOD	
1	03-02-2026	DA ISSUE	

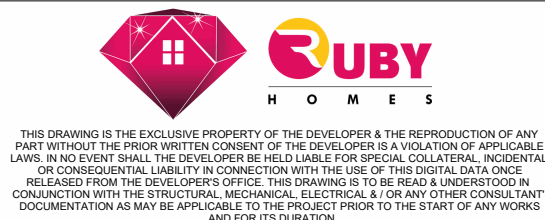

PROJECT:

LOT 2302 IN DP 1265815

161 MacDonald Rd
Bardia NSW

DRAWING TITLE:

GENERAL NOTES A

NORTH:

LOT NO:	DATE:	SCALE:	DRAWING No:	REV:
2302	1-10-2026		1 : 2	CC.02A
DRAWN BY:	CHECKED BY:	ISSUED BY:		
ROHIT	RH			
DRAFTED BY:	CLIENT NAME:			
rohit	Yuliana Chongbang			

TERMITE SHEET

- TERMITE SHEET EXTENDS THROUGH THE ENTIRE MASONRY LEAF AND IS VISIBLE AT THE FINISHED FACE OF THE WALL.


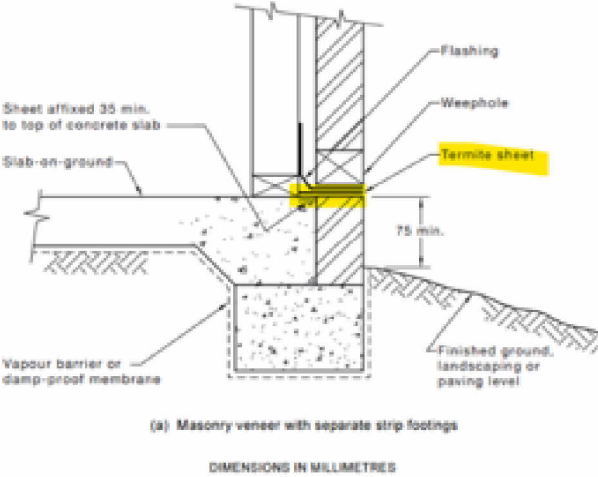


FIGURE 5.5 (in part) TYPICAL SHEET INSTALLATION TO EXTERNAL WALL WITH CONCRETE FLOOR SLAB

DPC FOR BRICKS

DAMP-PROOF COURSE (DPC) TO EXTENDS THROUGH THE ENTIRE MASONRY LEAF AND NEED TO BE VISIBLE AT THE FINISHED FACE OF THE WALL FROM OUTSIDE

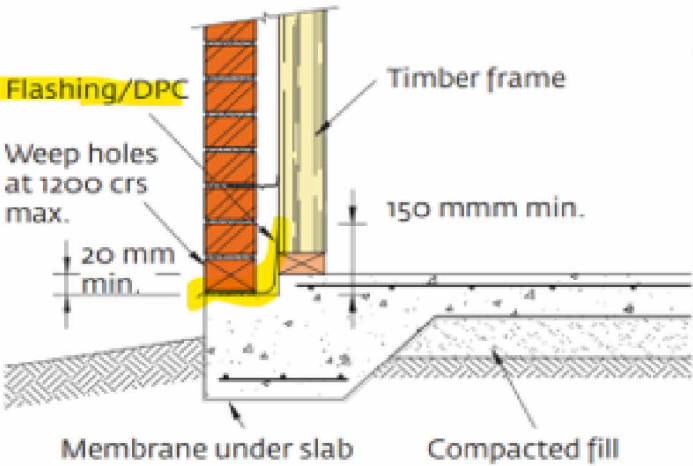

DEMOLITION

- AS 2601-2001 – DEMOLITION WORK

PLANTER BOX

REFER BELOW DETAILS FOR PLANTER BOX.



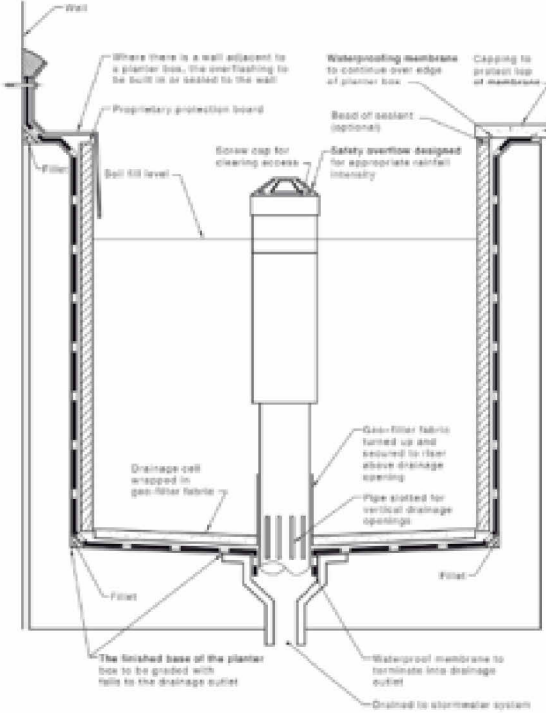


FIGURE 2.17 TYPICAL PLANTER BOX CONSTRUCTION

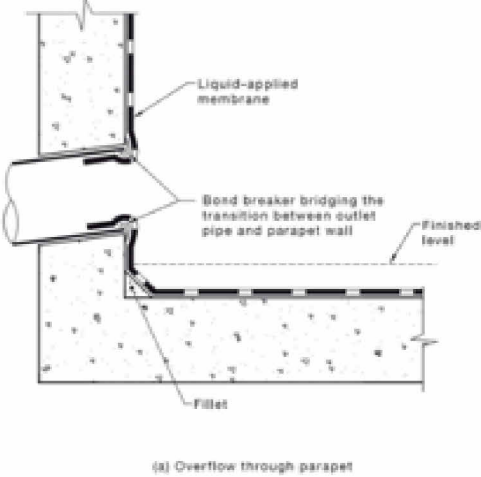

OVERFLOW TO BALCONY:

- SURFACE DRAIN & OVERFLOW TO BALCONY

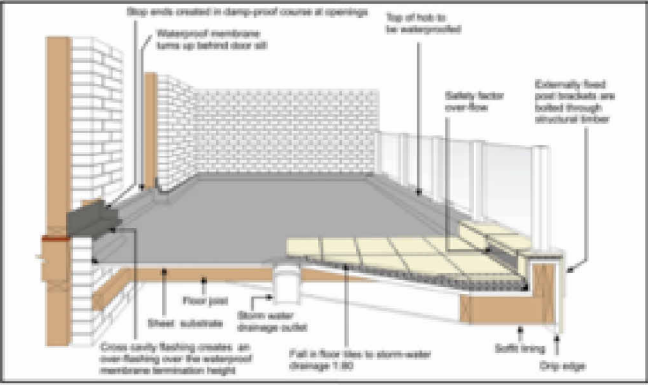

SWIMMING POOL

- PART 12.1.1 (H7D2) OF THE NCC VOLUME 2, AMENDMENT 1 - BUILDING CODE OF AUSTRALIA 2022 & HOUSING PROVISIONS STANDARD 2022
- AS 1926 PART 1-2012 – SWIMMING POOLSAFETY- SAFETY BARRIERS FOR SWIMMING POOLS
- AS 1926 PART 2-2007 - SWIMMING POOL SAFETY- LOCATION OF SAFETY BARRIERS FOR SWIMMING POOLS (INCORPORATING AMENDMENTS 1 AND 2)
- AS 1926 PART 3-2010 – SWIMMING POOL SAFETY- WATER RECIRCULATION SYSTEMS (INCORPORATING AMENDMENT 1)

REV	DATE	DESCRIPTION	BY
2	24-07-2026	DA MOD	
1	03-02-2026	DA ISSUE	

THIS DRAWING IS THE EXCLUSIVE PROPERTY OF THE DEVELOPER & THE REPRODUCTION OF ANY PART WITHOUT THE PRIOR WRITTEN CONSENT OF THE DEVELOPER IS A VIOLATION OF APPLICABLE LAWS. IN NO EVENT SHALL THE DEVELOPER BE HELD LIABLE FOR SPECIAL COLLATERAL, INCIDENTAL OR CONSEQUENTIAL LIABILITY IN CONNECTION WITH THE USE OF THIS DIGITAL DATA ONCE RELEASED FROM THE DEVELOPER'S OFFICE. THIS DRAWING IS TO BE READ & UNDERSTOOD IN CONJUNCTION WITH THE STRUCTURAL, MECHANICAL, ELECTRICAL & / OR ANY OTHER CONSULTANT'S DOCUMENTATION AS MAY BE APPLICABLE TO THE PROJECT PRIOR TO THE START OF ANY WORKS AND FOR ITS DURATION.

PROJECT:
LOT 2302 IN DP 1265815

161 MacDonald Rd
Bardia NSW

DRAWING TITLE:
GENERAL NOTES B

NORTH:

LOT NO:
2302
DRAWN BY:
ROHIT
DRAFTED BY:
rohit


DATE:
1-10-2026
CHECKED BY:
RH
CLIENT NAME:
Yuliana Chongbang

SCALE:
1 : 2


DRAWING No:
CC.02B

REV:
2
ISSUED BY:

CC ISSUE

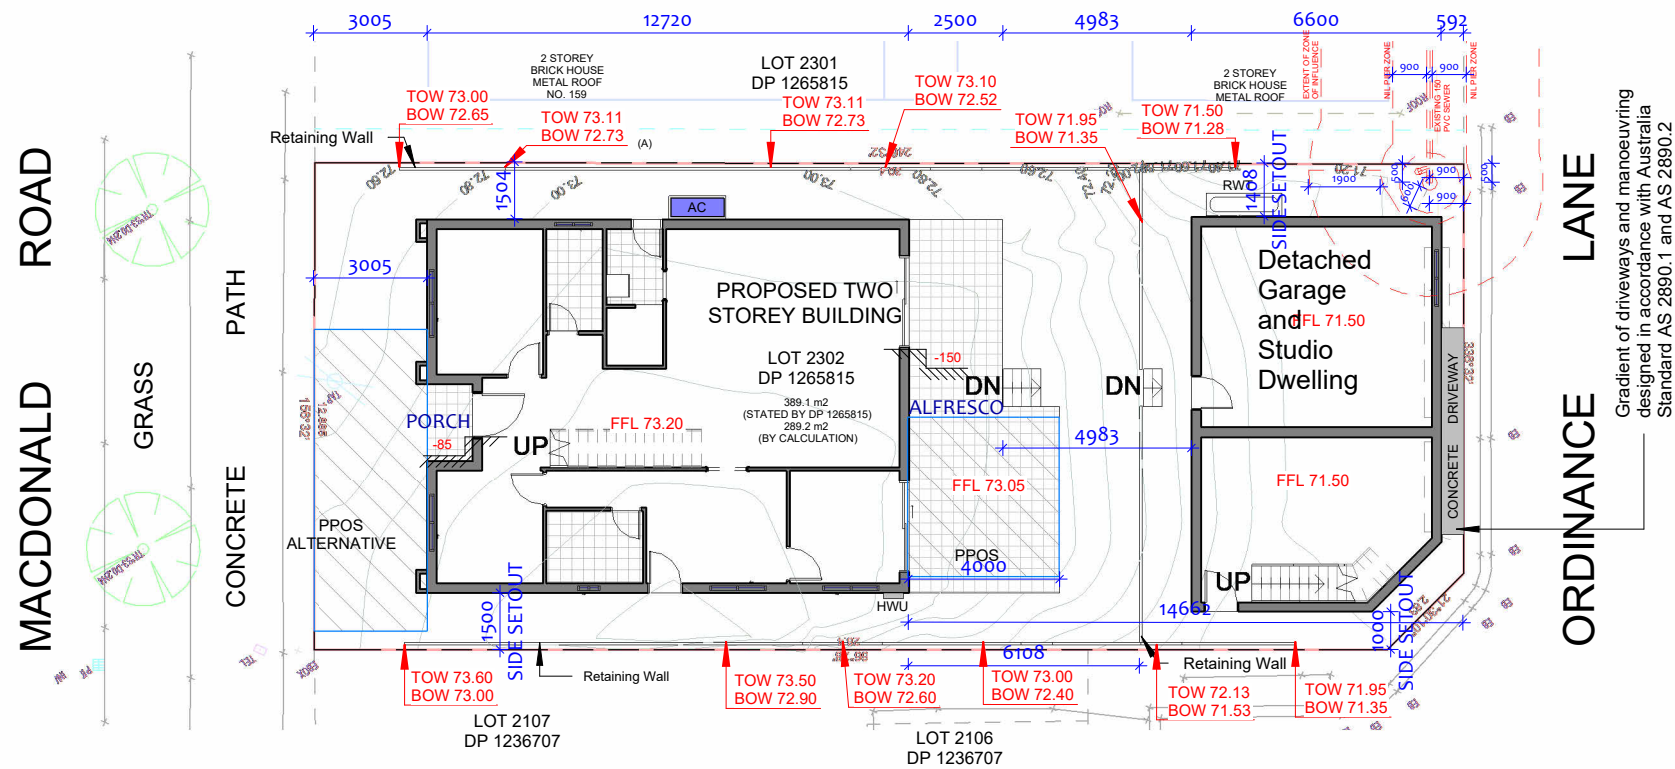

1 CC - SITE PLAN
1 : 200

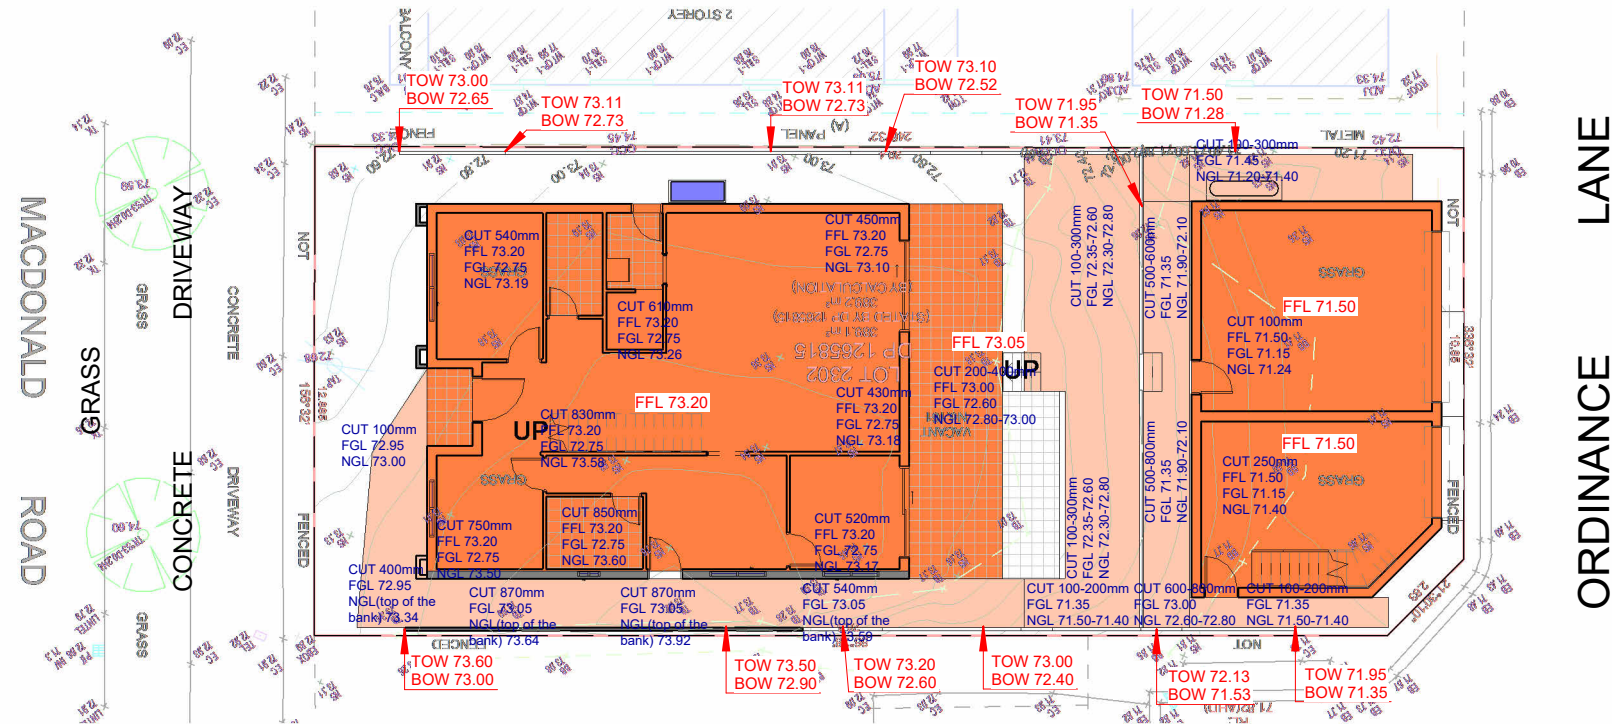

2 CUT AND FILL
1 : 200

Campbelltown Development Control Plan-
Campbelltown Edmonson Park South Development Control Plan 2012

DESCRIPTION		COMPLIANCE		COMMENT
ELEMENT	CODE CONTROL	REQUIREMNT	PROPOSED	
LAND ZONE	1 GENERAL RESIDENTIAL			
LOT NO	LOT 2302			
LOT AREA	389.10 m ²			
LOT WIDTH	Standard Lot Min. 6m at Building Line facing primary road		12.885 m	YES
HEIGHT	MAX. Height	9m	8m (MAX.)	YES
FRONT SETBACK	FRONT SET BACK (Min. Setback from Primary Road) For 300-350 sqm. Lot	3 m	3m	YES
REAR SET BACK (MIN.)	GROUND FLOOR	4m	11.5m	YES
	FIRST FLOOR	6m	14 m	
SIDE SET BACK (MIN.)	GROUND FLOOR	0.9m/0.9m	1.5/1.5m	YES
	FIRST FLOOR	0.9m/0.9m	1.5/1.5m	YES
COVERAGE AREA	55% of TOTAL LOT AREA	214 m ²	190 m ² (49%)	YES
PRIVATE OPEN SPACE	Min 16m ² with minimum dimension of 3m.	24m ²	24 m ²	YES
LANDSCAPE AREA	15 % of TOTAL LOT AREA	58.3 m ²	128.5m ²	YES
On-site car parking	One additional dedicated on-site car parking space		YES	
Principal Private open space	Balcony accessed directly off living space having minimum size of 8.0m ² with minimum dimension of 2m		YES	
Access	Separate direct access to a street, laneway		YES	
Services and facilities	on-site mail ,garbage storage area so that bins		YES	

(A) - EASEMENT FOR REPAIRS 0.9 WIDE (VIDE DP 1276530)

REV	DATE	DESCRIPTION	BY
2	24-07-2026	DA MOD	
1	03-02-2026	DA ISSUE	




THIS DRAWING IS THE EXCLUSIVE PROPERTY OF THE DEVELOPER & THE REPRODUCTION OF ANY PART WITHOUT THE PRIOR WRITTEN CONSENT OF THE DEVELOPER IS A VIOLATION OF APPLICABLE LAWS. IN NO EVENT SHALL THE DEVELOPER BE HELD LIABLE FOR SPECIAL COLLATERAL, INCIDENTAL OR CONSEQUENTIAL LIABILITY IN CONNECTION WITH THE USE OF THIS DIGITAL DATA ONCE RELEASED FROM THE DEVELOPER'S OFFICE. THIS DRAWING IS TO BE READ & UNDERSTOOD IN CONJUNCTION WITH THE STRUCTURAL, MECHANICAL, ELECTRICAL & / OR ANY OTHER CONSULTANT'S DOCUMENTATION AS MAY BE APPLICABLE TO THE PROJECT PRIOR TO THE START OF ANY WORKS AND FOR ITS DURATION.

PROJECT:
LOT 2302 IN DP 1265815


161 MacDonald Rd
Bardia NSW

DRAWING TITLE:
**LOCATION PLAN
AND SITE PLAN**

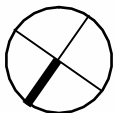NORTH:


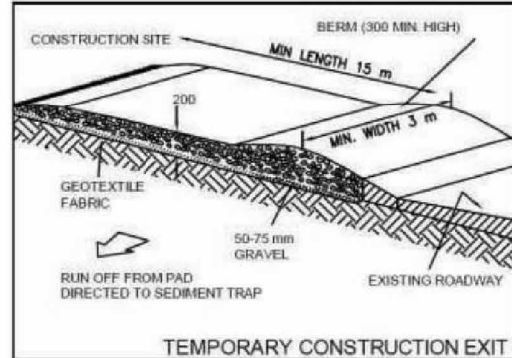
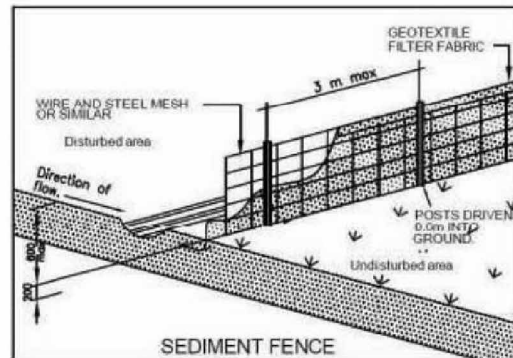
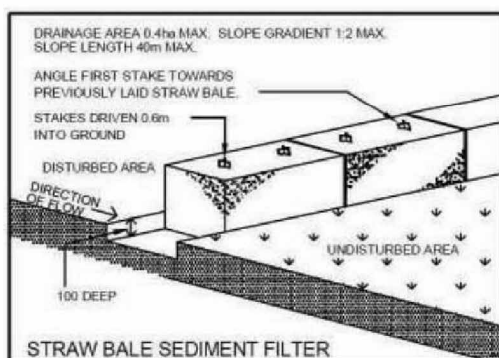
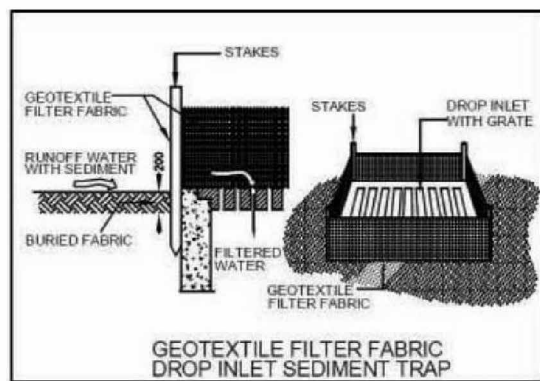
LOT NO: 2302	DATE: 1-10-2026	SCALE: As indicated	DRAWING No: CC.03	REV: 2
DRAWN BY: ROHIT	CHECKED BY: RH			ISSUED BY:
DRAFTED BY: rohit	CLIENT NAME: Yuliana Chongbang			

CC ISSUE

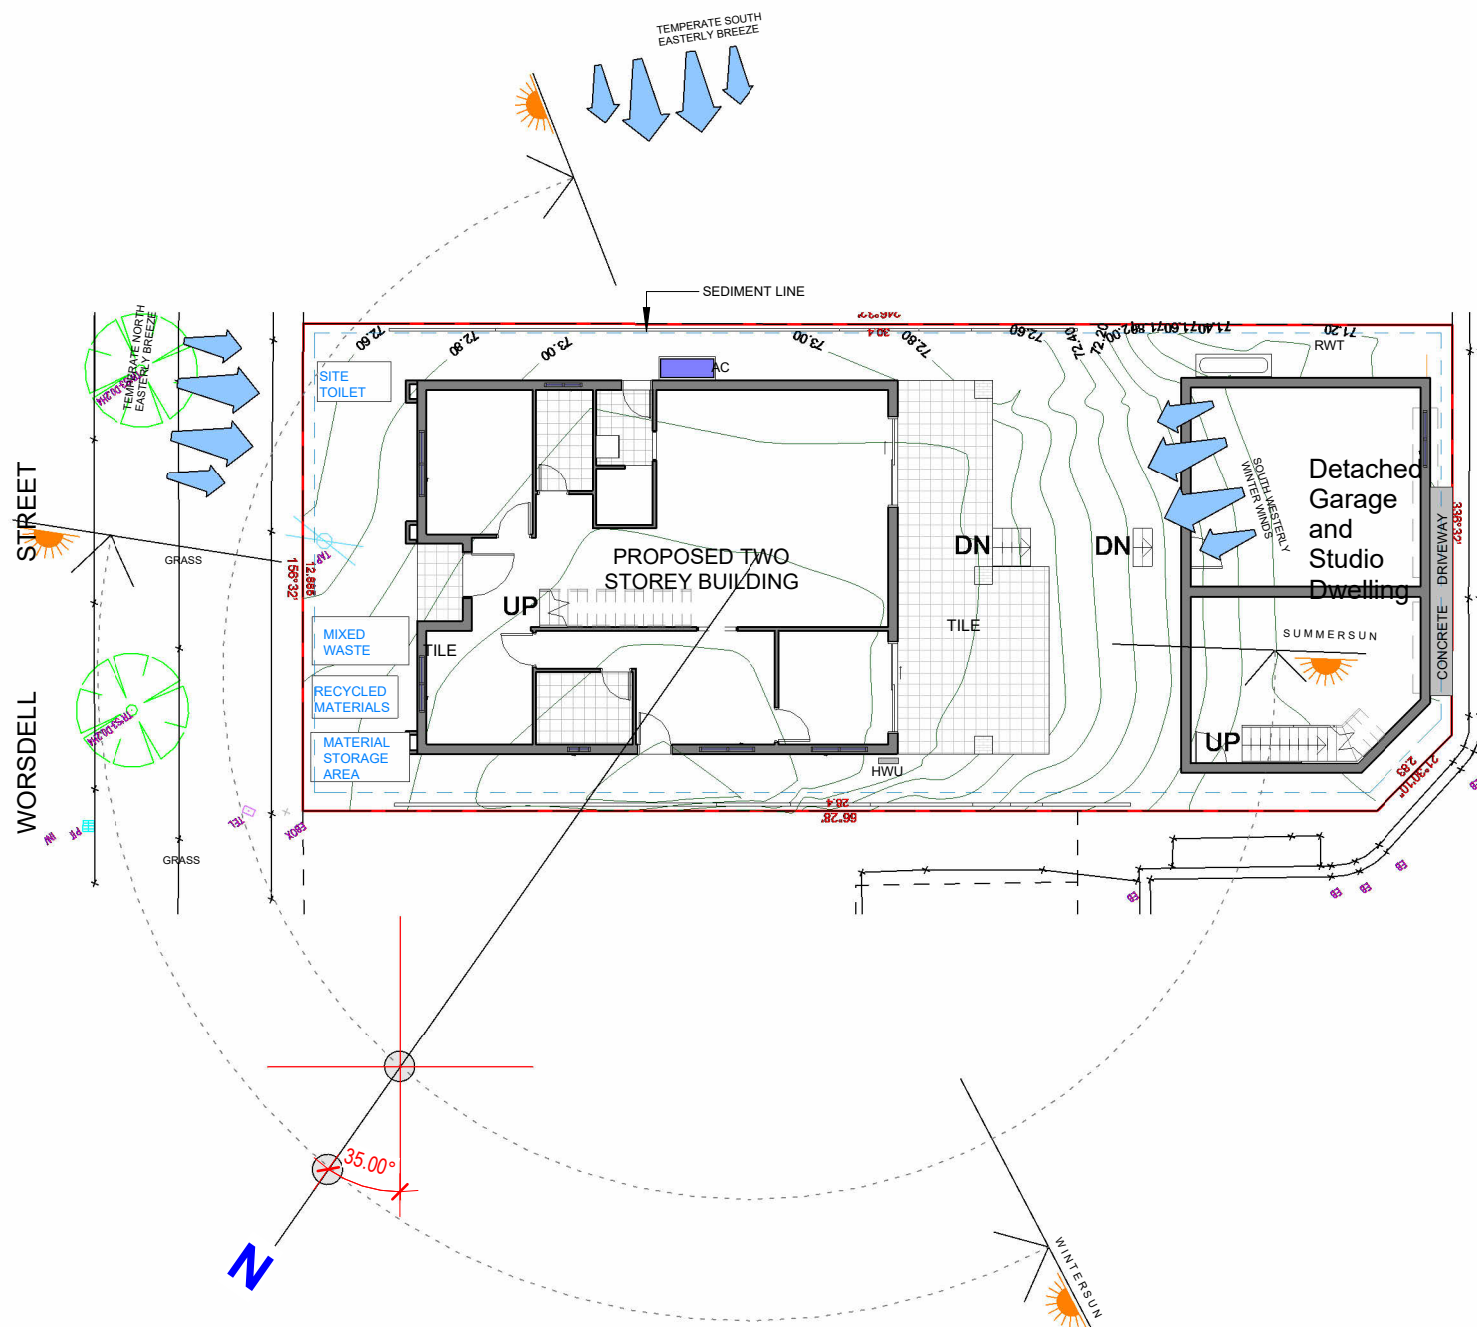

CC - SITE ANALYSIS AND SEDIMENT CONTROL

1
1 : 200



SEDIMENT AND EROSION NOTES:

- THIS PLAN TO BE READ IN CONJUNCTION WITH SEDIMENT AND EROSION CONTROL DETAILS AS ATTACHED.
- THE CONTRACTOR SHALL IMPLEMENT ALL SOIL EROSION AND SEDIMENT CONTROL MEASURES AS NECESSARY AND TO THE SATISFACTION OF COUNCIL PRIOR TO THE COMMENCEMENT AND DURING CONSTRUCTION. NO DISTURBANCE TO THE SITE SHALL BE PERMITTED OTHER THAN IN THE IMMEDIATE AREA OF THE WORK AND NO MATERIAL SHALL BE REMOVED FROM THE SITE WITHOUT COUNCIL'S APPROVAL. ALL SEDIMENT AND EROSION CONTROL DEVICES TO BE INSTALLED AND MAINTAINED IN ACCORDANCE WITH STANDARDS OUTLINED IN NSW DEPARTMENT OF HOUSING "MANAGING URBAN STORMWATER-SOILS AND CONSTRUCTIONS". TOPSOIL SHALL BE STRIPPED AND STOCKPILED OUTSIDE HAZARDOUS AREAS SUCH AS DRAINAGE LINES. THIS TOP SOIL IS TO BE RESPIRED LATER ON AREAS TO BE REVEGETATED AND STABILISED ONLY. (I.E ALL FOOTPATHS, BATTERS, SITE REGARDING AREAS, BASINS AND CATCH DRAINS). TOPSOIL SHALL NOT BE RESPIRED ON ANY OTHER AREAS UNLESS SPECIALLY INSTRUCTED BY THE SUPERIDENT. IF THEY ARE TO REMAIN FOR LONGER THAN ONE MONTH STOCKPILES SHALL BE PROTECTED FROM EROSION BY COVERING THEM WITH A MULCH AND HYDROSEEDING AND, IF NECESSARY, BY LOCATING BANKS OR DRAINS DOWNSTREAM OF A STOCKPILE TO RETARD SILT LADEN RUNOFF.
- THE CONTRACTOR SHALL REGULARLY MAINTAIN ALL SEDIMENT AND EROSION CONTROL DEVICES AND REMOVE ACCUMULATED SILT FROM SUCH DEVICES SUCH THAT MORE THAN 60% OF THEIR CAPACITY LOST. ALL THE SILTS TO BE PLACED OUTSIDE THE LIMIT OF WORKS. THE PERIOD FOR MAINTAINING THESE DEVICES SHALL BE AT LEAST UNTIL ALL DISTURBED AREAS ARE REVEGETATED AND FURTHER AS MAY BE DIRECTED BY THE SUPERINTENDENT OR COUNCIL.
- LAY TURF STRIP (MIN 300 mm WIDE) ON 100 mm TOPSOIL WITH 1.0 m LONG RETURNS EVERY 6.0m BEHIND ALL KERB AT THE TOP OF ALL BATTERS AND AROUND STRUCTURES IMMEDIATELY AFTER BACKFILLING OR FORMATION. THE CONTRACTOR SHALL GRASS SEED ALL DISTURBED AREAS WITH AN APPROVED MIX AS SSON AS PRACTICABLE AFTER COMPLETION OF EARTHWORKS AND REGRADING.
- VEHICULAR TRAFFIC SHALL BE CONTROLLED DURING CONSTRUCTION CONFINING ACCESS WHERE POSSIBLE TO NOMINATED STABILISED ACCESS POINTS.
- WHEN ANY DEVICES ARE TO BE HANDED OVER TO COUNCIL, THEY SHALL BE IN CLEAN AND STABLE CONDITION.
- THE CONTRACTOR SHALL IMPLEMENT DUST CONTROL BY REGULAR WETTING DOWN (BUT NOT SATURATING) DISTURBED AREA.
- PROVIDE AND MAINTAIN SILT TRAPS AROUND ALL SURFACE INLET PITS UNTIL CATCHMENT IS REVEGETATED OR PAVED.
- REVEGETATE ALL TRENCHES IMMEDIATELY UPON COMPLETION OF BACKFILLING.
- ALL DRAINAGE PIPE INLETS TO BE CAPPED UNTIL:
 - A) DOWNPIPES CONNECTED
 - B) PITS CONSTRUCTED & PROTECTED WITH SILT BARRIER

SITE WORKS NOTES

- ORIGIN OF LEVELS PROVIDED BY SURVEYOR
- THE BUILDER SHALL VERIFY ALL DIMENSIONS AND EXISTING LEVELS ON SITE PRIOR TO THE COMMENCEMENT OF WORK AND ANY DISCREPANCIES SHALL BE REPORTED TO THE SURVEYOR / ENGINEER.
- TOPSOIL SHALL BE STRIPPED FROM THE CONSTRUCTION AREA AND STOCKPILED ON SITE, TO BE LATER SPREAD OR DISPOSED OFF SITE AS DIRECTED BY SUPERVISOR / ENGINEER.
- ALL TH TRENCH BACKFILL MATERIAL SHALL BE COMPACTED TO THE SAME DENSITY AS THE ADJACENT MATERIAL.
- ALL SERVICE TRENCHES UNDER VEHICULAR PAVEMENTS SHALL BE BACKFILLED WITH SAND OR APPROVED GRANULAR MATERIALS TO THE UNDERSIDE OF THE PAVEMENT, AND COMPACTED TO 98% STANDARD MAXIMUM DRY DENSITY, IN ACCORDANCE WITH AS 1289E1.1.

TEMPORARY 1.8M HIGH WIRE ML FENCE WITH DUSTPROOF MESH APPLIED TO FULL HEIGHT TO BOUNDARIES AS REQUIRED

LOCATION OF WASTE BINS

SEDIMENT FENCE AS REQUIRED

GRAVEL ACCESS

SITE ACCESS AREA TO BE USED FOR WASHDOWN AREA

FOOTPATH CLEAN AND CLEAR AT ALL TIMES

LOCATION OF STOCKPILE MATERIAL

MATERIAL STORAGE AREA

TEMPORARY TOILETS

INSTALL TEMPORARY SEDIMENT BARRIERS TO ALL INLET PITS LIKELY TO COLLECT SILT LADEN WATER, TO COUNCIL'S REQUIREMENTS.

SD 5-7 STABILISED SITE ACCESS

- STRIP TOPSOIL AND LEVEL SITE.
- COMPACT SUBGRADE.
- COVER AREA WITH GEOTEXTILE.
- CONSTRUCT 200 mm THICK PAD OVER GEOTEXTILE USING ROADBASE OR 30 mm AGGREGATE. Min 15 m LONG OR TO BUILDING ALIGNMENT. Min 3 m WIDE.
- CONSTRUCT HUMP IMMEDIATELY WITHIN BOUNDARY TO DIVERT WATER TO A SEDIMENT FENCE OR OTHER SEDIMENT TRAP.

SD 6-9 GEOTEXTILE INLET FILTER

- FABRICATE A SEDIMENT BARRIER MADE FROM GEOTEXTILE. REFER SD6-7 FOR DETAILS.
- SUPPORT GEOTEXTILE WITH MESH TIED TO POSTS AT 1 m Ctrs.
- DO NOT COVER INLET WITH GEOTEXTILE.

CC ISSUE

REV	DATE	DESCRIPTION	BY
2	24-07-2026	DA MOD	
1	03-02-2026	DA ISSUE	




RUBY
HOMES

THIS DRAWING IS THE EXCLUSIVE PROPERTY OF THE DEVELOPER & THE REPRODUCTION OF ANY PART WITHOUT THE PRIOR WRITTEN CONSENT OF THE DEVELOPER IS A VIOLATION OF APPLICABLE LAWS. IN NO EVENT SHALL THE DEVELOPER BE HELD LIABLE FOR SPECIAL COLLATERAL, INCIDENTAL OR CONSEQUENTIAL LIABILITY IN CONNECTION WITH THE USE OF THIS DIGITAL DATA ONCE RELEASED FROM THE DEVELOPER'S OFFICE. THIS DRAWING IS TO BE READ & UNDERSTOOD IN CONJUNCTION WITH THE STRUCTURAL, MECHANICAL, ELECTRICAL & / OR ANY OTHER CONSULTANT'S DOCUMENTATION AS MAY BE APPLICABLE TO THE PROJECT PRIOR TO THE START OF ANY WORKS AND FOR ITS DURATION.

PROJECT:
LOT 2302 IN DP 1265815

161 MacDonald Rd
Bardia NSW

DRAWING TITLE:
**SITE ANALYSIS
AND SEDIMENT
CONTROL**

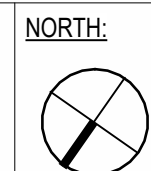

LOT NO:	DATE:	SCALE:	DRAWING No:	REV:
2302	1-10-2026	As indicated	CC.04	2
DRAWN BY:	CHECKED BY:	CLIENT NAME:	ISSUED BY:	
ROHIT	RH	Yuliana Chongbang		

Table 6.1.1: Minimum construction requirements

Component	Minimum Rw dB(A) Values Required	Indicative Treatment Required	Rw dB(A) of Indicative Treatment Specified
External Walls	37	(Red Book CSR 5877) Brick façade, wall wrap, 40mm cavity, 70mm timber studs at 600mm maximum centres, 10mm Gyprock Plus Plasterboard internal	57
Roof/Ceiling	35	(Red Book CSR 6402) Sheet metal roof, 60 MD Bradford Anticon insulation, 40mm battens, timber ceiling joists at 600mm maximum centres, 165 Gold Batts, 10mm Gyprock Plus plasterboard	41
Windows (sliding)	30	(AWS Series 504) 10mm glass Sliding window with acoustic seals ¹	31

Windows (fixed)	21	4mm monolithic glass with acoustic seals ¹	31
Sliding Doors	34	(AWS Series 541) 10.38mm Laminated Glass with full perimeter acoustic seals ¹	35
Entry Door	29	45mm thick solid core wood (particleboard or blockboard) door with full perimeter acoustic seals ¹ , any glazing to be minimum 10.38mm laminate glass	33



¹Acoustic seals shall be a Schlegel Q-Lon seal or an equivalent product; mohair seals are not acceptable.

6.2.1 Ducting

To maintain the acoustic performance of the building envelope the first 3m of duct should be internally lined with minimum 50mm acoustic insulation. The duct should have no dimension greater than 300mm and the inlet acoustically sealed into the eaves.

- (3) Two leaves of 110 mm clay brick masonry with—
(a) a cavity not less than 50 mm between leaves; and
(b) 13 mm cement render on each outside face,
has an $R_w + C_{tr}$ of not less than 50, if constructed in accordance with Figure 10.7.5b.

Figure 10.7.5b: Two leaves of 110 mm clay brick masonry (method 2)

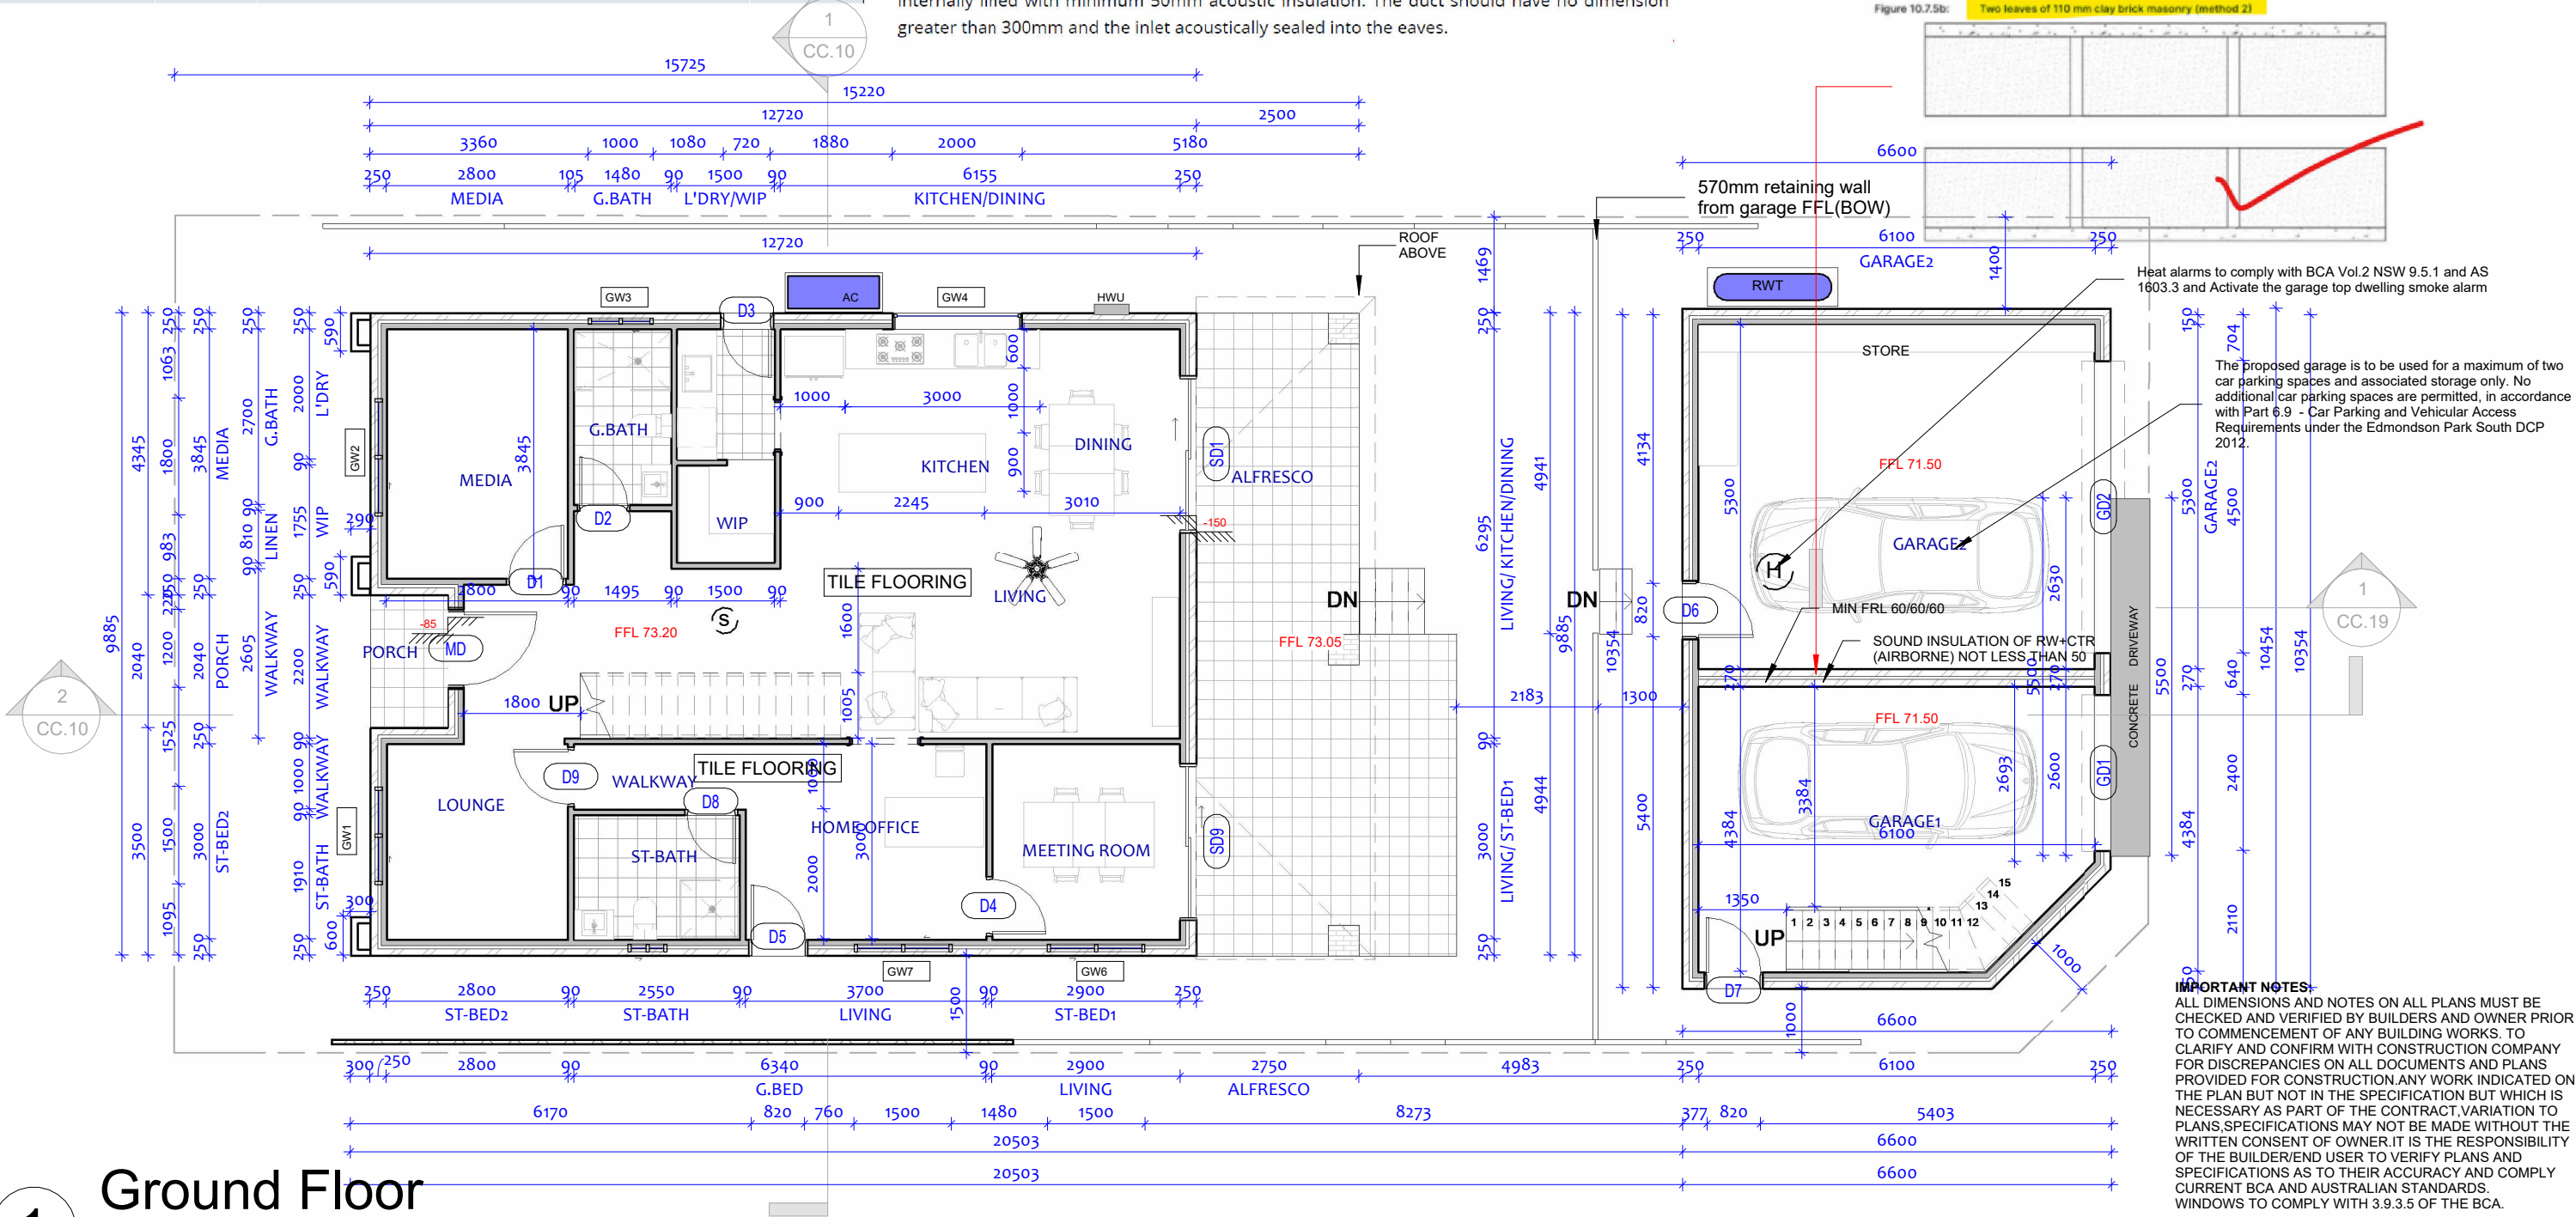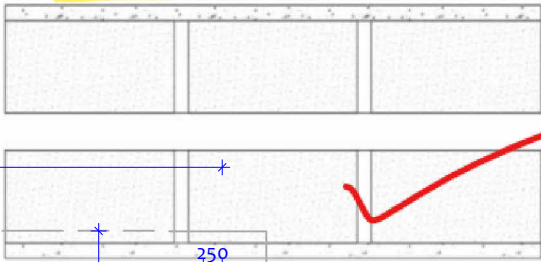

Heat alarms to comply with BCA Vol.2 NSW 9.5.1 and AS 1603.3 and Activate the garage top dwelling smoke alarm

The proposed garage is to be used for a maximum of two car parking spaces and associated storage only. No additional car parking spaces are permitted, in accordance with Part 6.9 - Car Parking and Vehicular Access Requirements under the Edmondson Park South DCP 2012.

IMPORTANT NOTES:
ALL DIMENSIONS AND NOTES ON ALL PLANS MUST BE CHECKED AND VERIFIED BY BUILDERS AND OWNER PRIOR TO COMMENCEMENT OF ANY BUILDING WORKS. TO CLARIFY AND CONFIRM WITH CONSTRUCTION COMPANY FOR DISCREPANCIES ON ALL DOCUMENTS AND PLANS PROVIDED FOR CONSTRUCTION. ANY WORK INDICATED ON THE PLAN BUT NOT IN THE SPECIFICATION BUT WHICH IS NECESSARY AS PART OF THE CONTRACT, VARIATION TO PLANS, SPECIFICATIONS MAY NOT BE MADE WITHOUT THE WRITTEN CONSENT OF OWNER. IT IS THE RESPONSIBILITY OF THE BUILDER/END USER TO VERIFY PLANS AND SPECIFICATIONS AS TO THEIR ACCURACY AND COMPLY CURRENT BCA AND AUSTRALIAN STANDARDS. WINDOWS TO COMPLY WITH 3.9.3.5 OF THE BCA.

1 Ground Floor
1 : 100

REV	DATE	DESCRIPTION	BY
2	24-07-2026	DA MOD	
1	03-02-2026	DA ISSUE	

RUBY HOMES

THIS DRAWING IS THE EXCLUSIVE PROPERTY OF THE DEVELOPER & THE REPRODUCTION OF ANY PART WITHOUT THE PRIOR WRITTEN CONSENT OF THE DEVELOPER IS A VIOLATION OF APPLICABLE LAWS. IN NO EVENT SHALL THE DEVELOPER BE HELD LIABLE FOR SPECIAL COLLATERAL, INCIDENTAL OR CONSEQUENTIAL LIABILITY IN CONNECTION WITH THE USE OF THIS DIGITAL DATA ONCE RELEASED FROM THE DEVELOPER'S OFFICE. THIS DRAWING IS TO BE READ & UNDERSTOOD IN CONJUNCTION WITH THE STRUCTURAL, MECHANICAL, ELECTRICAL & / OR ANY OTHER CONSULTANT'S DOCUMENTATION AS MAY BE APPLICABLE TO THE PROJECT PRIOR TO THE START OF ANY WORKS AND FOR ITS DURATION.



PROJECT:
LOT 2302 IN DP 1265815

161 MacDonald Rd
Bardia NSW

DRAWING TITLE:
GROUND FLOOR PLAN



NORTH:

LOT NO: 2302	DATE: 1-10-2026	SCALE: 1 : 100	DRAWING No: CC.05	REV: 2
DRAWN BY: ROHIT	CHECKED BY: RH			ISSUED BY:
DRAFTED BY: rohit	CLIENT NAME: Yuliana Chongbang			

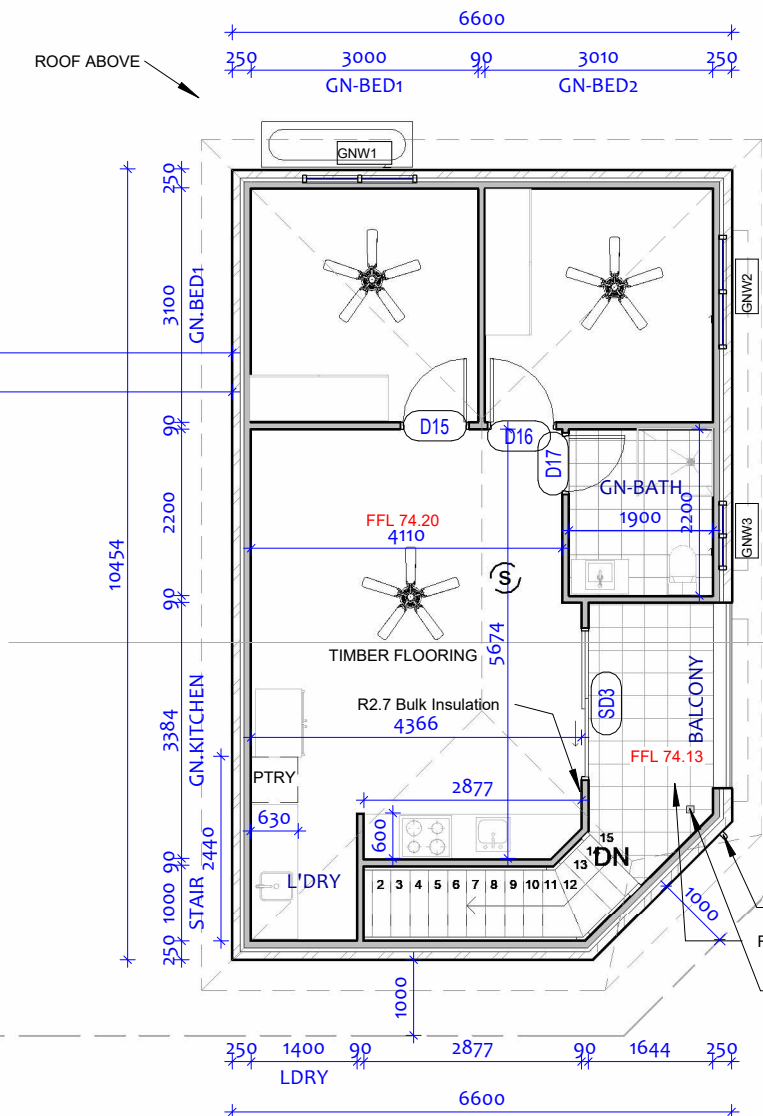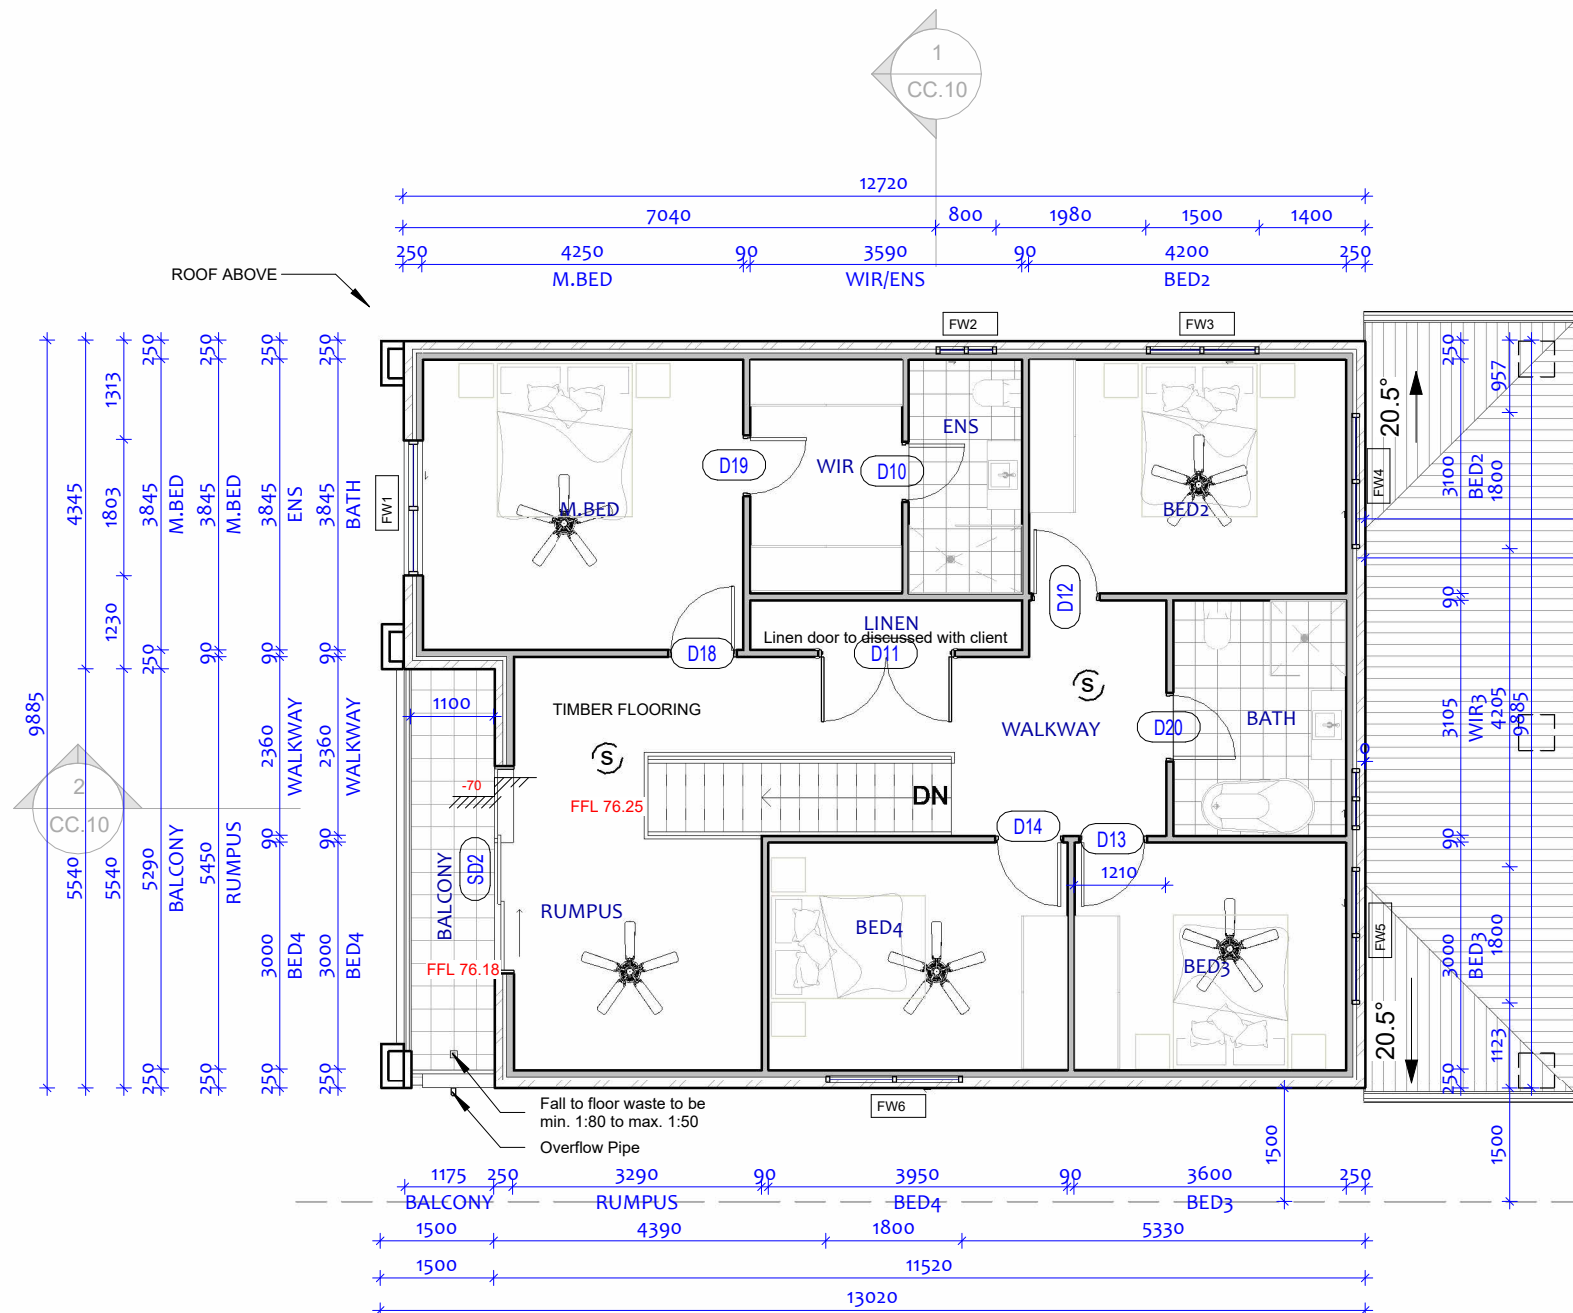

IMPORTANT NOTES:
ALL DIMENSIONS AND NOTES ON ALL PLANS MUST BE CHECKED AND VERIFIED BY BUILDERS AND OWNER PRIOR TO COMMENCEMENT OF ANY BUILDING WORKS. TO CLARIFY AND CONFIRM WITH CONSTRUCTION COMPANY FOR DISCREPANCIES ON ALL DOCUMENTS AND PLANS PROVIDED FOR CONSTRUCTION. ANY WORK INDICATED ON THE PLAN BUT NOT IN THE SPECIFICATION BUT WHICH IS NECESSARY AS PART OF THE CONTRACT, VARIATION TO PLANS, SPECIFICATIONS MAY NOT BE MADE WITHOUT THE WRITTEN CONSENT OF OWNER. IT IS THE RESPONSIBILITY OF THE BUILDER/END USER TO VERIFY PLANS AND SPECIFICATIONS AS TO THEIR ACCURACY AND COMPLY CURRENT BCA AND AUSTRALIAN STANDARDS. WINDOWS TO COMPLY WITH 3.9.3.5 OF THE BCA.

Figure 16: Party Wall over Masonry Wall - Plan View

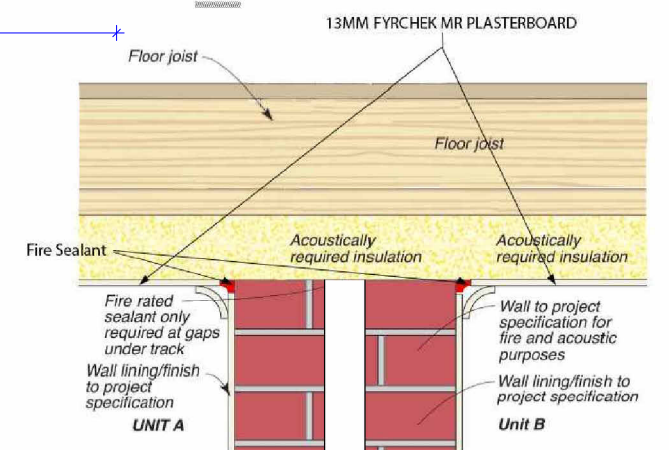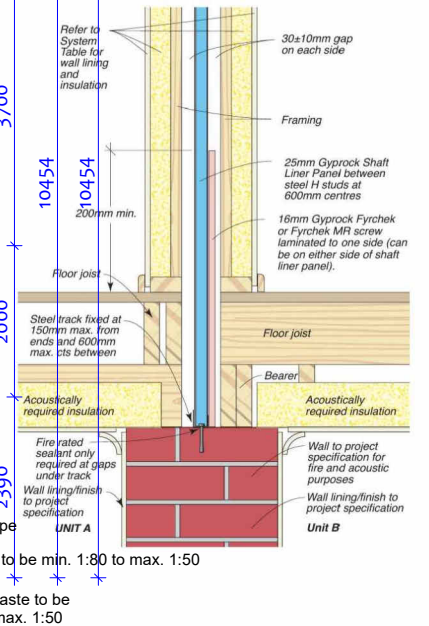

1 Level 1
1 : 100

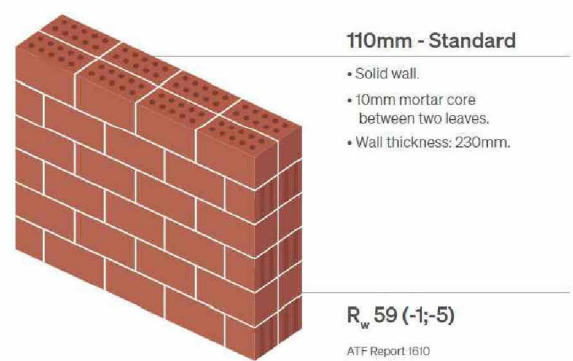


Table 1: Gyprock Plasterboard Features, Applications & Specifications

GYPROCK® PLASTERBOARDS	APPLICATIONS – WALLS & CEILINGS	THICK-NESS (mm)	MASS kg/m ²	FIRE GRADE	MOISTURE RESISTANT	ENHANCED IMPACT RESISTANCE	ENHANCED SOUND RESISTANCE	ENHANCED SOUND ABSORPTION	MOULD RESISTANT	LOW VOC	CECA ACCREDITED
	FEATURES										
Soundchek™	- Designed to provide enhanced acoustic resistance. - A machine made sheet composed of a high density gypsum core encased in a heavy duty linerboard. - Long edges are recessed for flush jointing.	13	13.0				✓			✓	CECA
Impactchek™	- Fire grade board reinforced with a woven fibreglass mesh to produce a high strength plasterboard which resists soft body impact damage. - Ideal for high traffic areas such as hallways, stairways, playrooms and garages. - Long edges are recessed for flush jointing.	13	10.5	✓		✓	✓			✓	CECA
Fyrchek™	- Fire grade board composed of a specially processed glass fibre reinforced gypsum core encased in a heavy duty linerboard. - Ideal for high performance fire and acoustic rated walls and ceilings. - Long edges are recessed for flush jointing.	13	10.5	✓			✓			✓	CECA
		16	12.5								
Fyrchek™ MR	- Fire grade board with moisture resistant properties. - Both the core and the liner board are treated in manufacture to withstand the effects of high humidity and moisture. - Long edges are recessed for flush jointing.	13	10.8	✓	✓		✓			✓	CECA
		16	12.9	✓						✓	

REV	DATE	DESCRIPTION	BY
2	24-07-2026	DA MOD	
1	03-02-2026	DA ISSUE	

RUBY HOMES

THIS DRAWING IS THE EXCLUSIVE PROPERTY OF THE DEVELOPER & THE REPRODUCTION OF ANY PART WITHOUT THE PRIOR WRITTEN CONSENT OF THE DEVELOPER IS A VIOLATION OF APPLICABLE LAWS. IN NO EVENT SHALL THE DEVELOPER BE HELD LIABLE FOR SPECIAL COLLATERAL, INCIDENTAL OR CONSEQUENTIAL LIABILITY IN CONNECTION WITH THE USE OF THIS DIGITAL DATA ONCE RELEASED FROM THE DEVELOPER'S OFFICE. THIS DRAWING IS TO BE READ & UNDERSTOOD IN CONJUNCTION WITH THE STRUCTURAL, MECHANICAL, ELECTRICAL & / OR ANY OTHER CONSULTANT'S DOCUMENTATION AS MAY BE APPLICABLE TO THE PROJECT PRIOR TO THE START OF ANY WORKS AND FOR ITS DURATION.


PROJECT:
LOT 2302 IN DP 1265815

161 MacDonald Rd
Bardia NSW

DRAWING TITLE:
FIRST FLOOR LEVEL

NORTH:

LOT NO: 2302	DATE: 1-10-2026	SCALE: 1 : 100	DRAWING No: CC.06	REV: 2
DRAWN BY: ROHIT	CHECKED BY: RH			ISSUED BY:
DRAFTED BY: rohit	CLIENT NAME: Yuliana Chongbang			

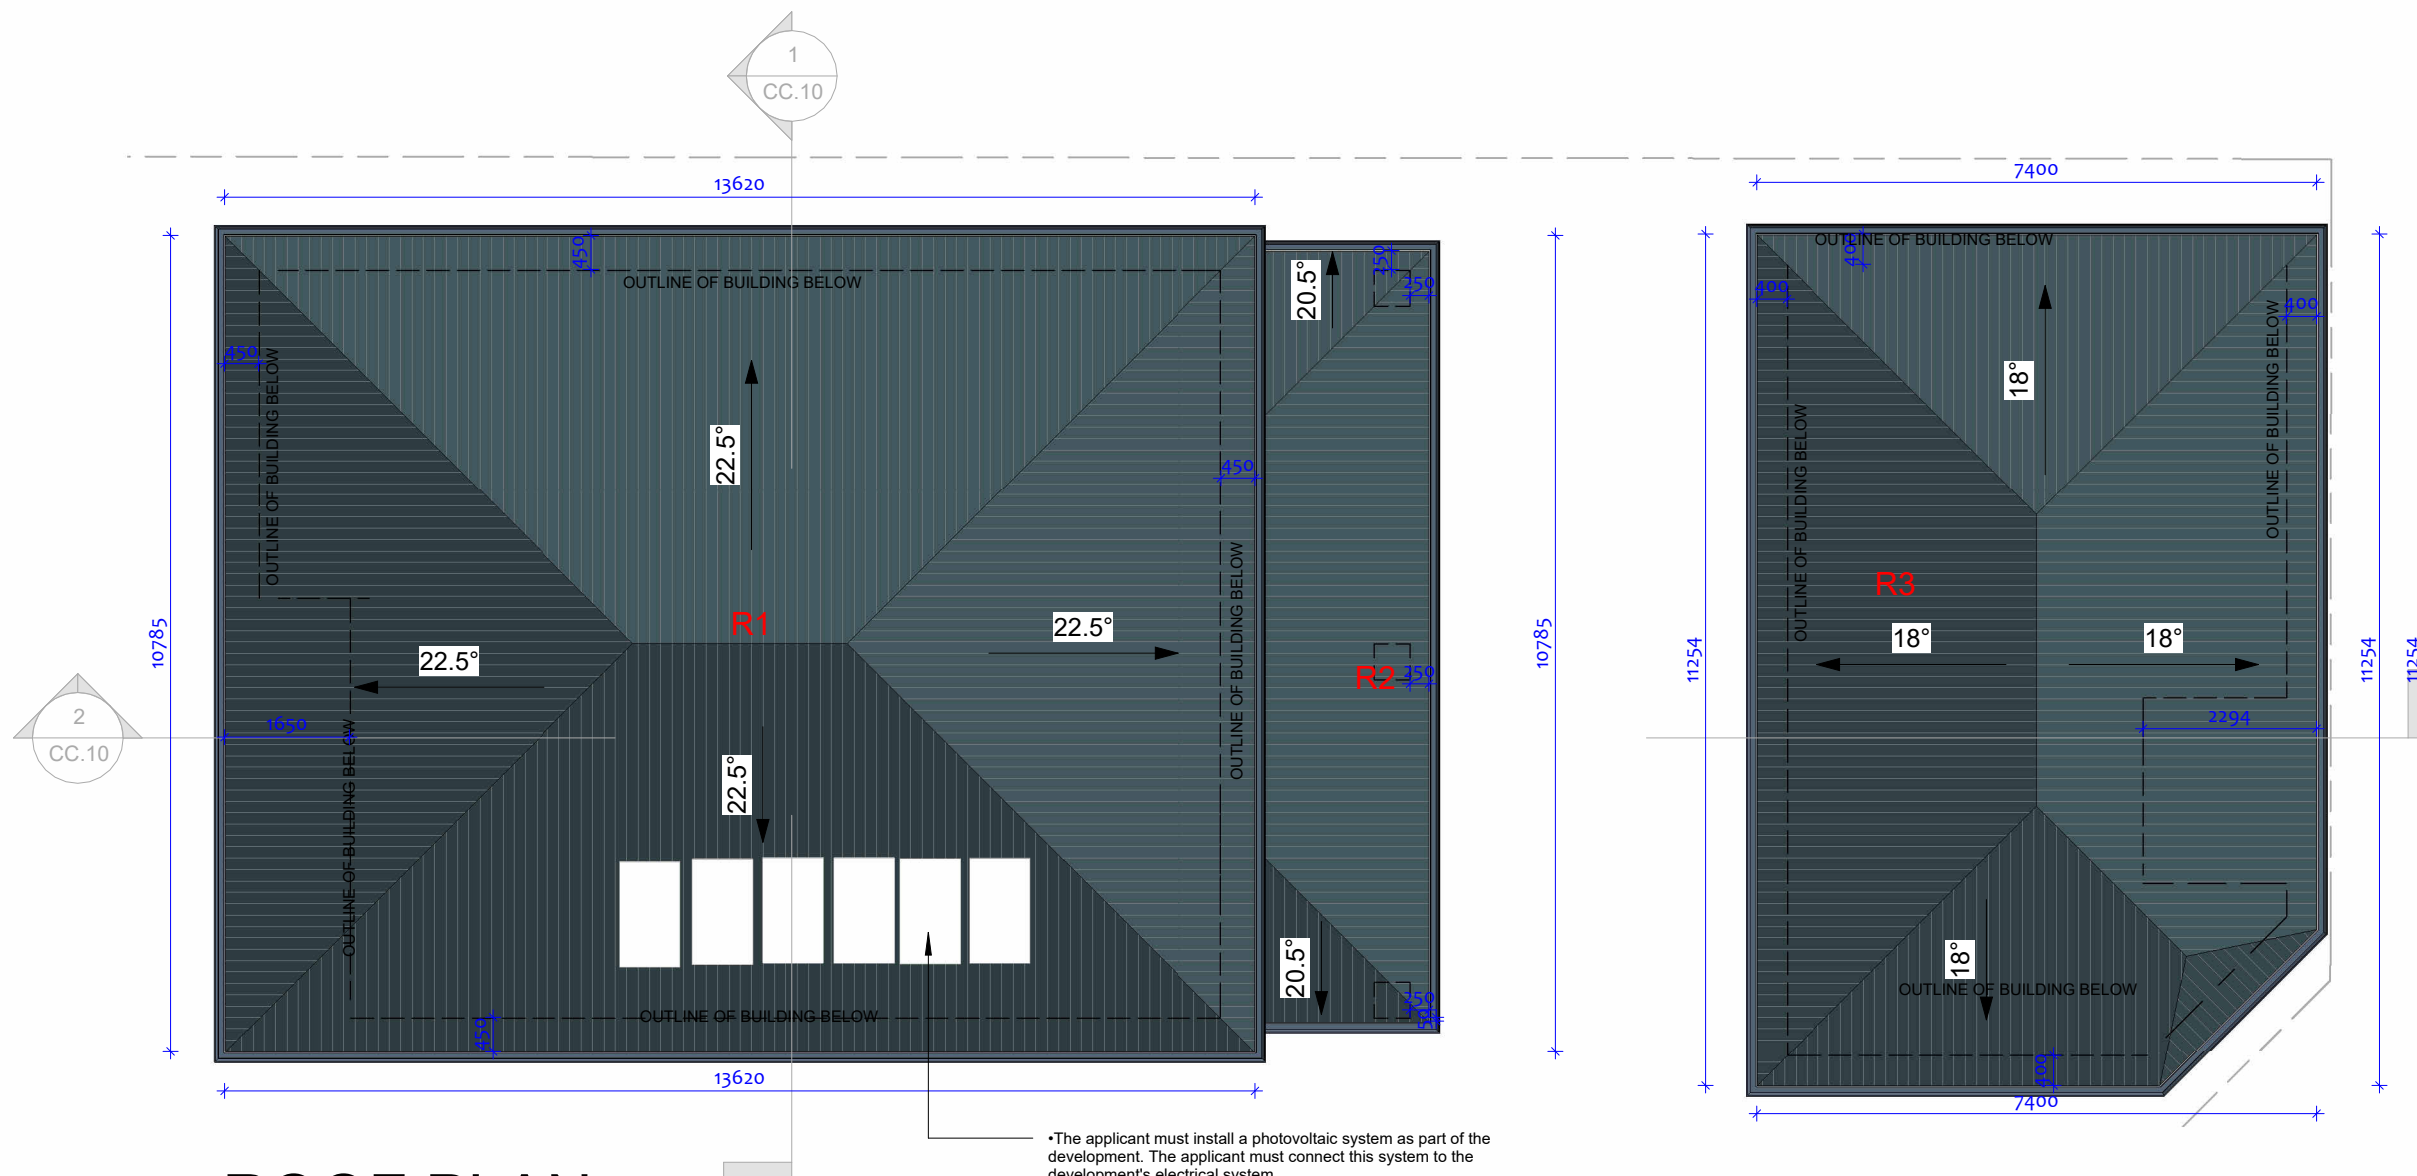

IMPORTANT NOTES:
ALL DIMENSIONS AND NOTES ON ALL PLANS MUST BE CHECKED AND VERIFIED BY BUILDERS AND OWNER PRIOR TO COMMENCEMENT OF ANY BUILDING WORKS. TO CLARIFY AND CONFIRM WITH CONSTRUCTION COMPANY FOR DISCREPANCIES ON ALL DOCUMENTS AND PLANS PROVIDED FOR CONSTRUCTION. ANY WORK INDICATED ON THE PLAN BUT NOT IN THE SPECIFICATION BUT WHICH IS NECESSARY AS PART OF THE CONTRACT, VARIATION TO PLANS, SPECIFICATIONS MAY NOT BE MADE WITHOUT THE WRITTEN CONSENT OF OWNER. IT IS THE RESPONSIBILITY OF THE BUILDER/END USER TO VERIFY PLANS AND SPECIFICATIONS AS TO THEIR ACCURACY AND COMPLY CURRENT BCA AND AUSTRALIAN STANDARDS. WINDOWS TO COMPLY WITH 3.9.3.5 OF THE BCA.

ABCB HOUSING PROVISIONS STANDARD 2022


10.8.3 VENTILATION OF ROOF SPACES

1. IN CLIMATE ZONES 6, 7 AND 8, A ROOF MUST HAVE A ROOF SPACE THAT
- (A) IS LOCATED
- (I) IMMEDIATELY ABOVE THE *PRIMARY INSULATION LAYER*, OR
- (II) IMMEDIATELY ABOVE SARKING WITH A *VAPOUR PERMEANCE* OF NOT LESS THAN 1.14 $\mu\text{G/N.S.}$, IMMEDIATELY ABOVE THE *PRIMARY INSULATION LAYER*, OR
- (III) IMMEDIATELY ABOVE CEILING INSULATION MEETS THE REQUIREMENTS OF 13.2.3(3) AND 13.2.3(4); AND
- (B) HAS A HEIGHT OF NOT LESS THAN 20MM; AND
- (C) IS EITHER -
- (I) VENTILATED TO OUTDOOR AIR THROUGH EVENLY DISTRIBUTED OPENINGS IN ACCORDANCE WITH TABLE 10.8.3; OR
- (II) LOCATED IMMEDIATELY UNDERNEATH THE ROOF TILES OF A UNSARKED TILED ROOF.

Table 10.8.3: Roof space ventilation requirements


Roof pitch	Ventilation openings
< 10°	25,000 mm ² /m provided at each of two opposing ends
≥ 10° and < 15°	25,000 mm ² /m provided at the eaves and 5,000 mm ² /m at high level
≥ 15° and < 75°	7,000 mm ² /m provided at the eaves and 5,000 mm ² /m at high level, plus an additional 18,000 mm ² /m at the eaves if the roof has a cathedral ceiling


Figure 10.8.3 (explanatory): Example of roof space with low level ventilation

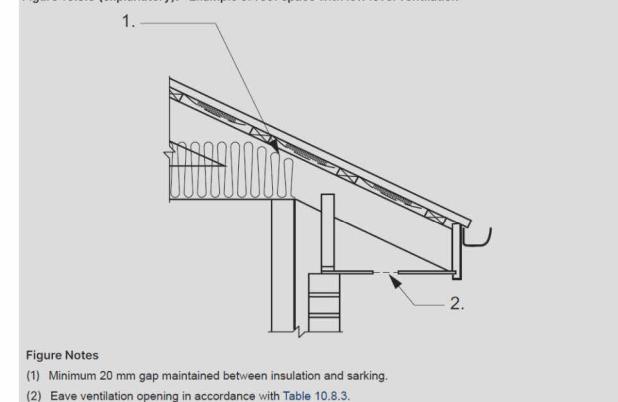

Roof Schedule			
Mark	Base Level	Area	Comments
R1	CEILING LEVEL	159 m ²	ROOF COLORBOND
R2	Level 1	30 m ²	ROOF COLORBOND
R3	GN FL CEILING	85 m ²	ROOF COLORBOND
Grand total: 3		274 m ²	


CC ISSUE

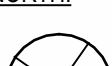				 THIS DRAWING IS THE EXCLUSIVE PROPERTY OF THE DEVELOPER & THE REPRODUCTION OF ANY PART WITHOUT THE PRIOR WRITTEN CONSENT OF THE DEVELOPER IS A VIOLATION OF APPLICABLE LAWS. IN NO EVENT SHALL THE DEVELOPER BE HELD LIABLE FOR SPECIAL, COLLATERAL, INCIDENTAL OR CONSEQUENTIAL LIABILITY IN CONNECTION WITH THE USE OF THIS DIGITAL DATA ONCE RELEASED FROM THE DEVELOPER'S OFFICE. THIS DRAWING IS TO BE READ & UNDERSTOOD IN CONJUNCTION WITH THE STRUCTURAL, MECHANICAL, ELECTRICAL & / OR ANY OTHER CONSULTANT'S DOCUMENTATION AS MAY BE APPLICABLE TO THE PROJECT PRIOR TO THE START OF ANY WORKS AND FOR ITS DURATION.	PROJECT: LOT 2302 IN DP 1265815 161 MacDonald Rd Bardia NSW	DRAWING TITLE: ROOF PLAN	NORTH: 	LOT NO: 2302	DATE: 1-10-2026	SCALE: 1 : 100	DRAWING No: CC.07	REV: 2
DRAWN BY: ROHIT	CHECKED BY: RH	ISSUED BY:										
DRAFTED BY: rohit	CLIENT NAME: Yuliana Chongbang											
2	24-07-2026	DA MOD										
1	03-02-2026	DA ISSUE										
REV	DATE	DESCRIPTION	BY									

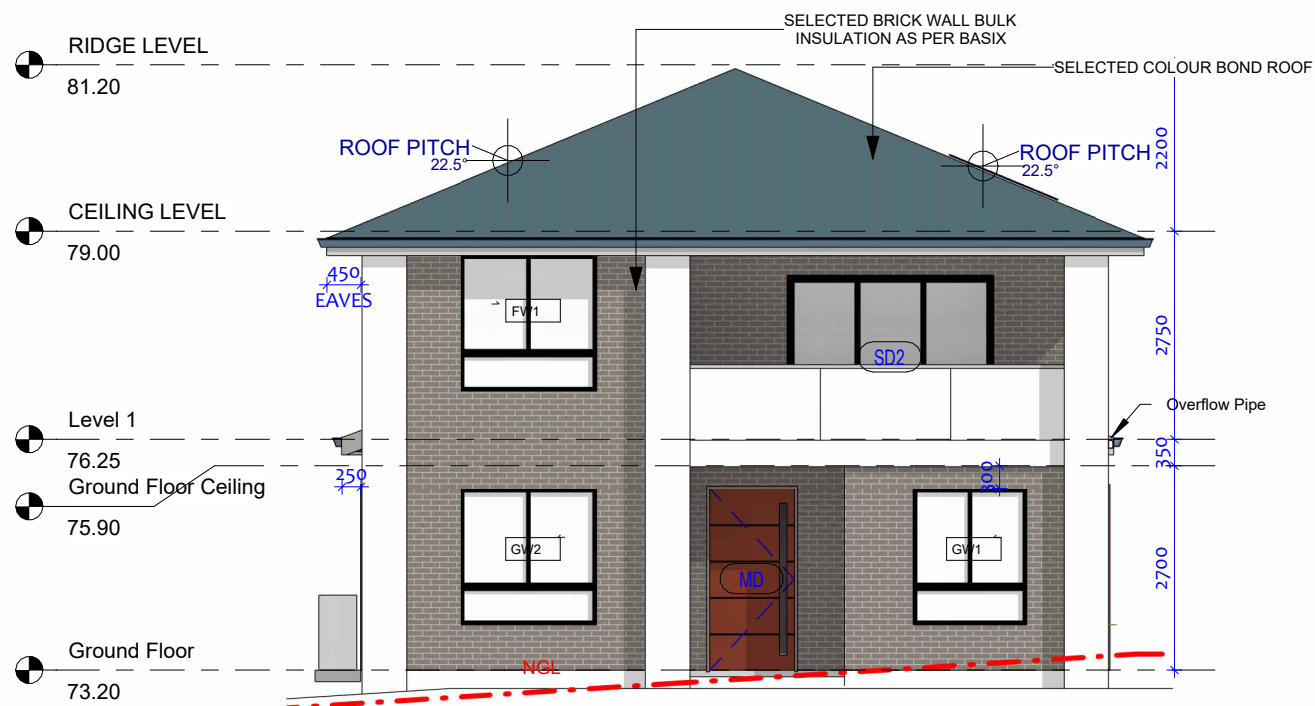


NORTH-EAST ELEVATION

1
1 : 100

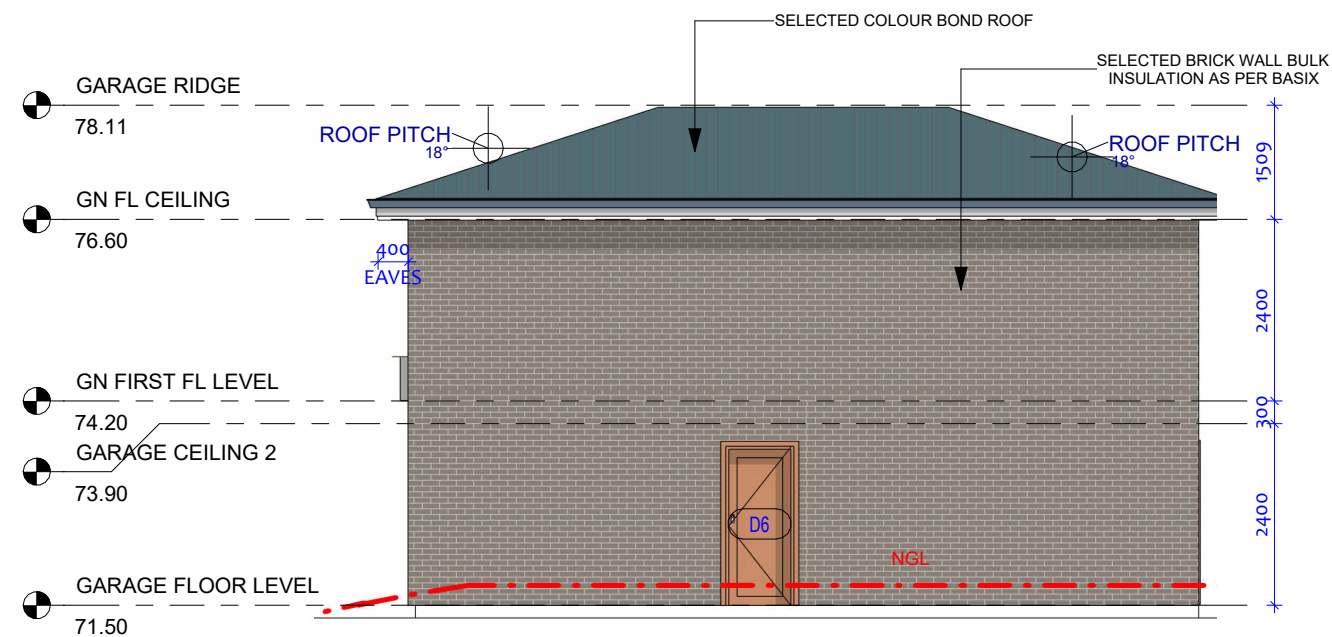


NORTH-WEST ELEVATION GRANNY

4
1 : 100

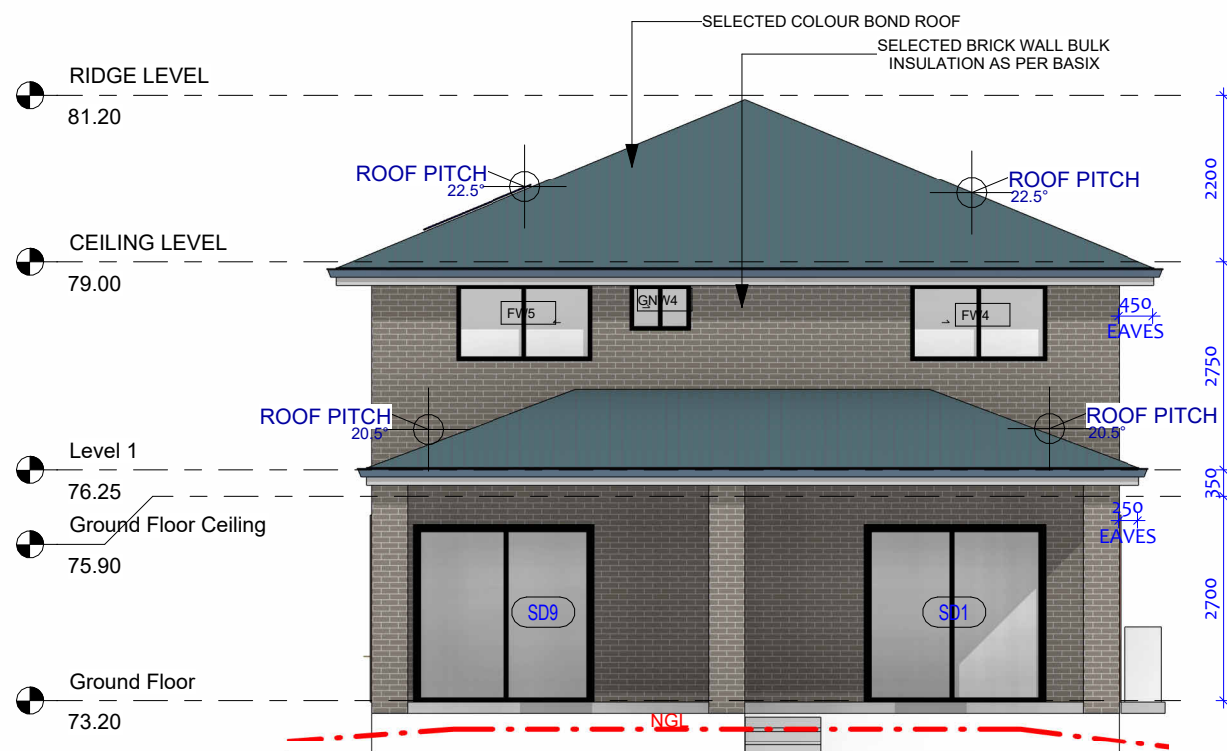

SOUTH-WEST ELEVATION

2
1 : 100

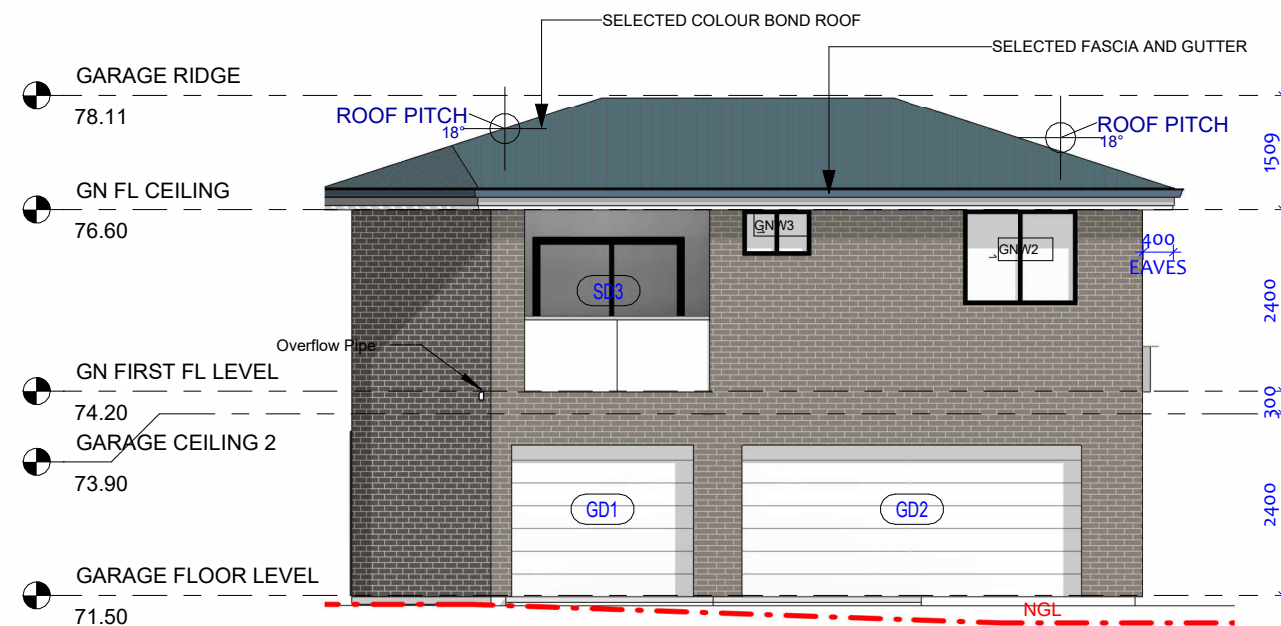

SOUTH-WEST ELEVATION GRANNY

3
1 : 100


REV	DATE	DESCRIPTION	BY
2	24-07-2026	DA MOD	
1	03-02-2026	DA ISSUE	



THIS DRAWING IS THE EXCLUSIVE PROPERTY OF THE DEVELOPER & THE REPRODUCTION OF ANY PART WITHOUT THE PRIOR WRITTEN CONSENT OF THE DEVELOPER IS A VIOLATION OF APPLICABLE LAWS. IN NO EVENT SHALL THE DEVELOPER BE HELD LIABLE FOR SPECIAL COLLATERAL, INCIDENTAL OR CONSEQUENTIAL LIABILITY IN CONNECTION WITH THE USE OF THIS DIGITAL DATA ONCE RELEASED FROM THE DEVELOPER'S OFFICE. THIS DRAWING IS TO BE READ & UNDERSTOOD IN CONJUNCTION WITH THE STRUCTURAL, MECHANICAL, ELECTRICAL & / OR ANY OTHER CONSULTANT'S DOCUMENTATION AS MAY BE APPLICABLE TO THE PROJECT PRIOR TO THE START OF ANY WORKS AND FOR ITS DURATION.

PROJECT: LOT 2302 IN DP 1265815		DRAWING TITLE: ELEVATION 01		NORTH:		LOT NO: 2302		DATE: 1-10-2026		SCALE: 1 : 100		DRAWING No: CC.08		REV: 2	
161 MacDonald Rd Bardia NSW						DRAWN BY: ROHIT		CHECKED BY: RH						ISSUED BY:	
						DRAFTED BY: rohit		CLIENT NAME: Yuliana Chongbang							


CC ISSUE

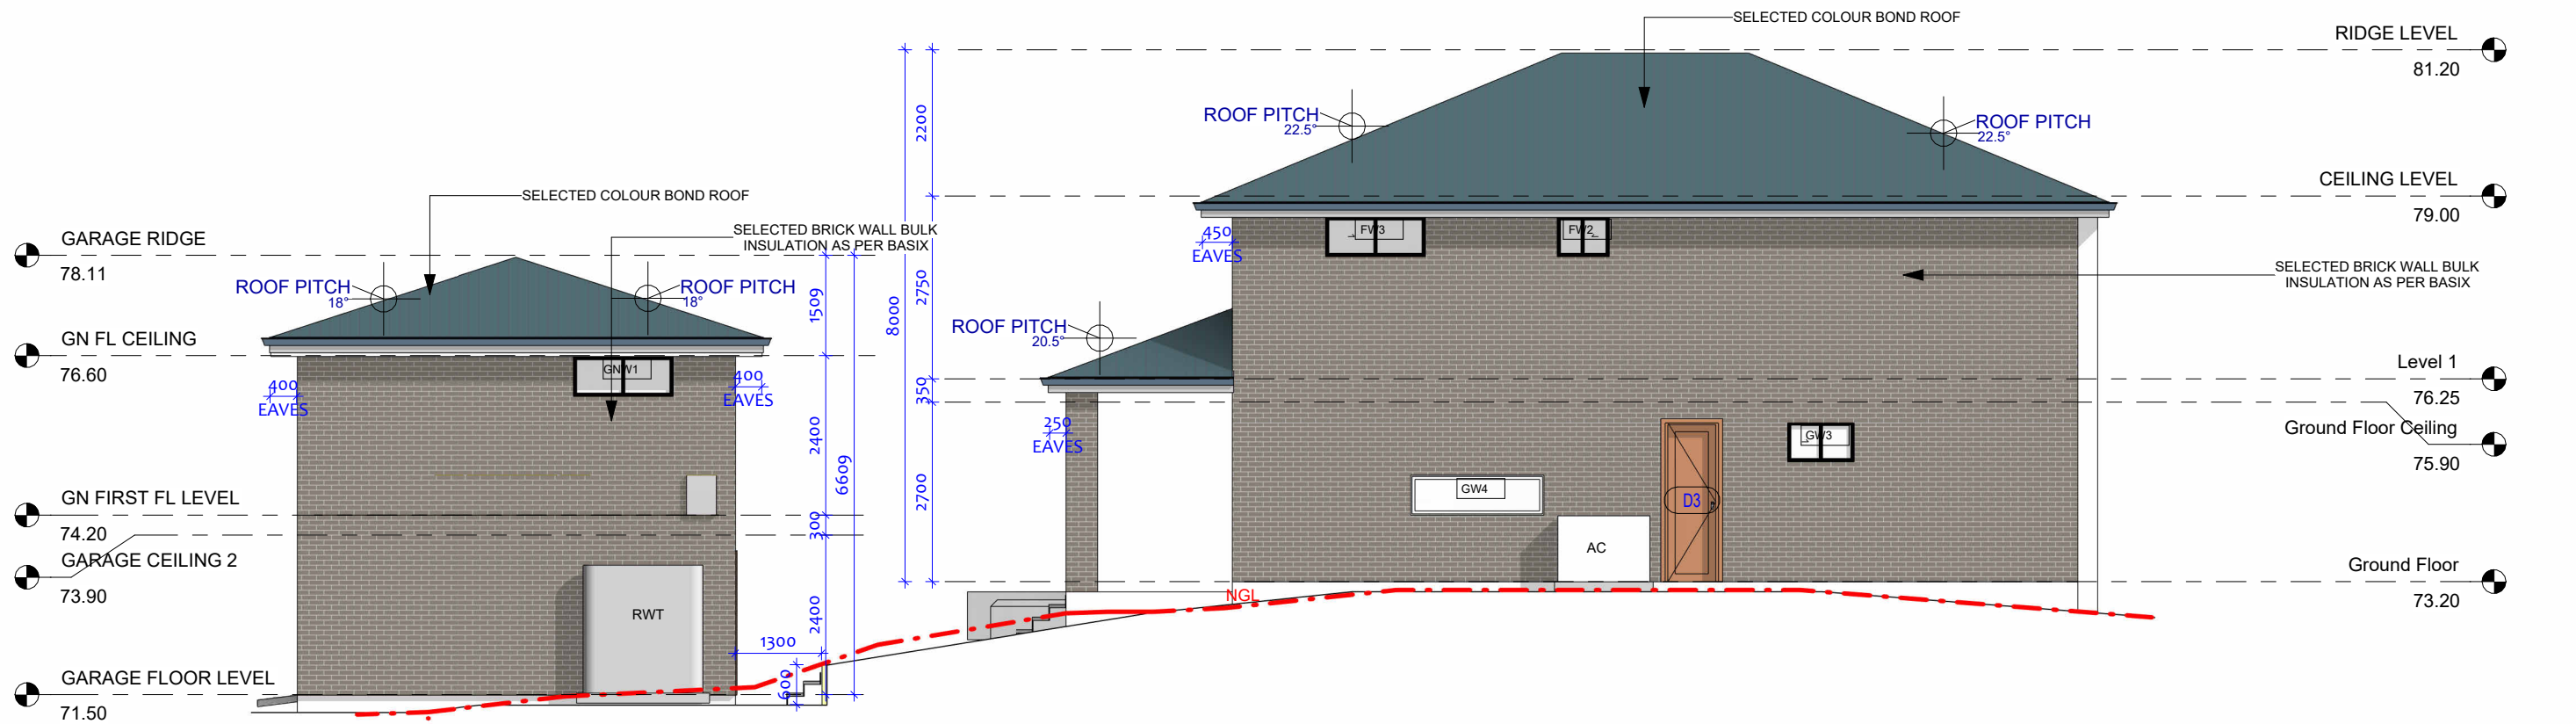

SOUTH EAST ELEVATION

1

1 : 100

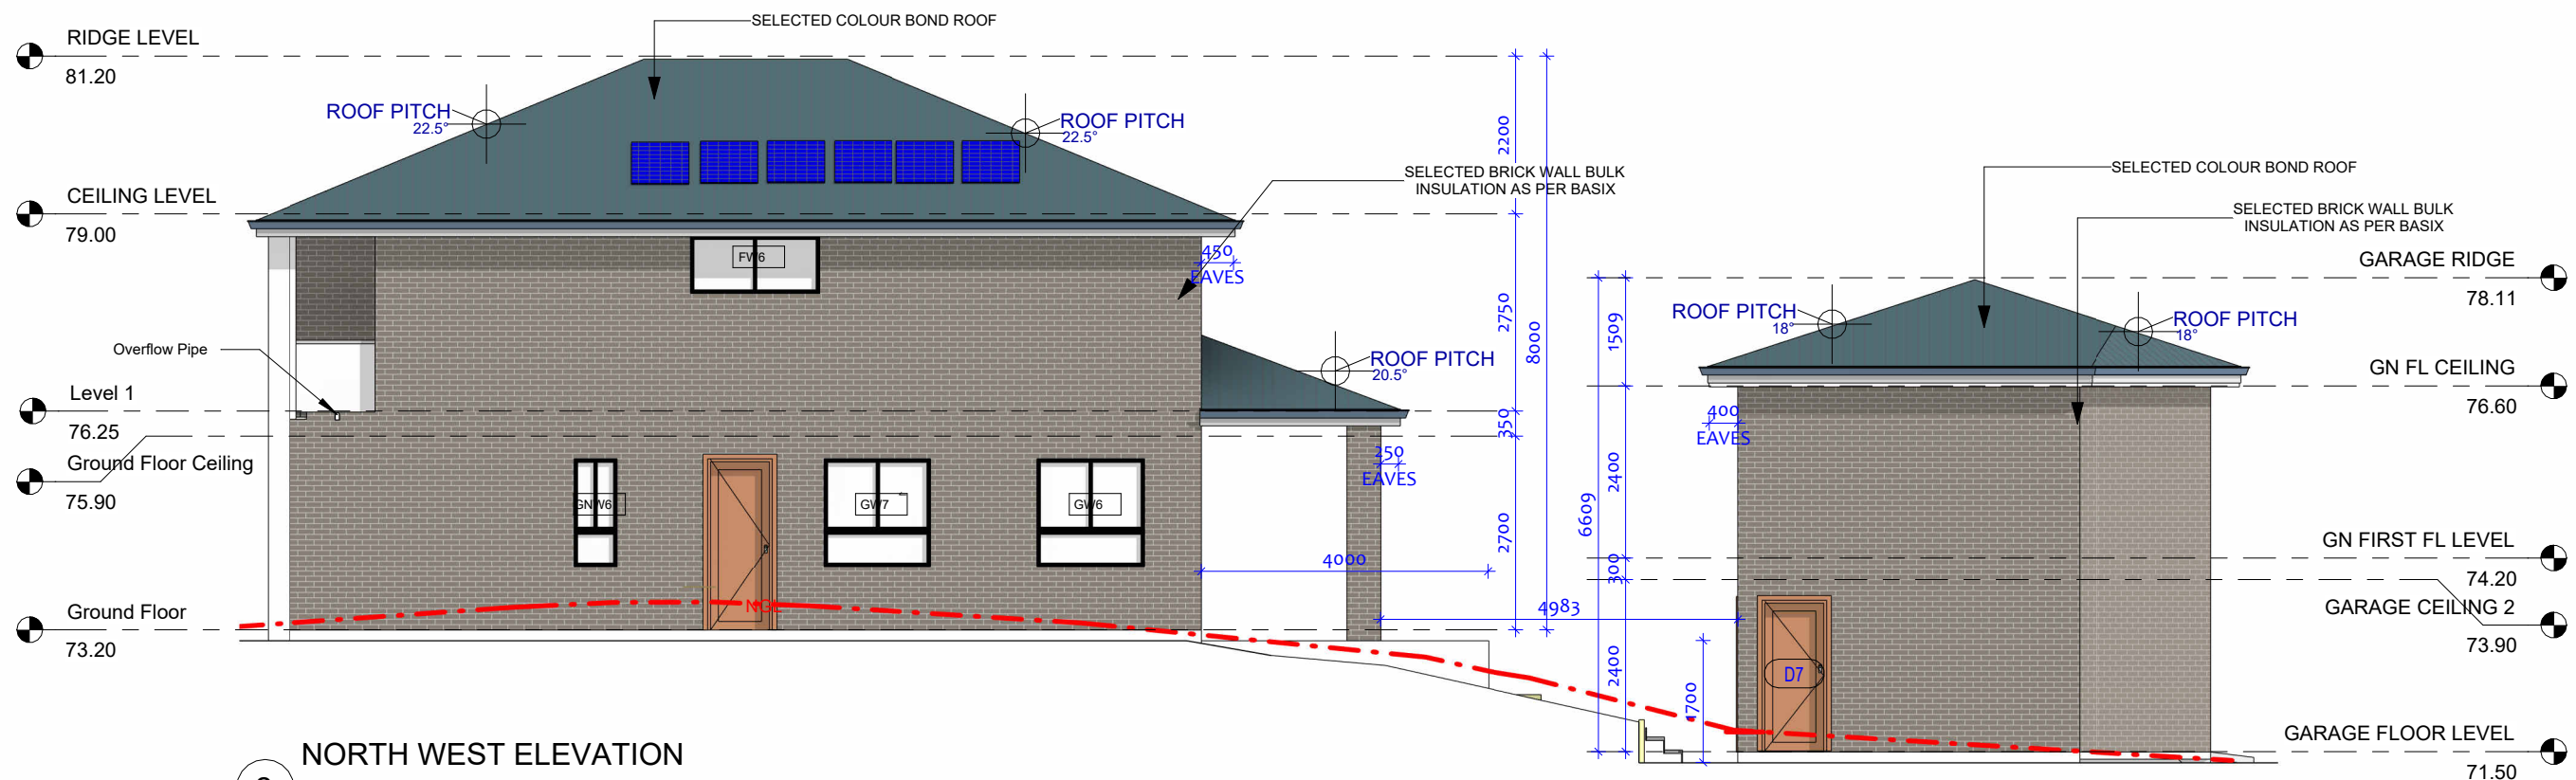

NORTH WEST ELEVATION

2

1 : 100

REV	DATE	DESCRIPTION	BY
2	24-07-2026	DA MOD	
1	03-02-2026	DA ISSUE	


RUBY HOMES


THIS DRAWING IS THE EXCLUSIVE PROPERTY OF THE DEVELOPER & THE REPRODUCTION OF ANY PART WITHOUT THE PRIOR WRITTEN CONSENT OF THE DEVELOPER IS A VIOLATION OF APPLICABLE LAWS. IN NO EVENT SHALL THE DEVELOPER BE HELD LIABLE FOR SPECIAL COLLATERAL, INCIDENTAL OR CONSEQUENTIAL LIABILITY IN CONNECTION WITH THE USE OF THIS DIGITAL DATA ONCE RELEASED FROM THE DEVELOPER'S OFFICE. THIS DRAWING IS TO BE READ & UNDERSTOOD IN CONJUNCTION WITH THE STRUCTURAL, MECHANICAL, ELECTRICAL & / OR ANY OTHER CONSULTANT'S DOCUMENTATION AS MAY BE APPLICABLE TO THE PROJECT PRIOR TO THE START OF ANY WORKS AND FOR ITS DURATION.

PROJECT:
LOT 2302 IN DP 1265815

161 MacDonald Rd
Bardia NSW

DRAWING TITLE:
ELEVATION 02

NORTH:	LOT NO:	DATE:	SCALE:	DRAWING No:	REV:
	2302	1-10-2026			2
	DRAWN BY:	CHECKED BY:	1 : 100	CC.09	ISSUED BY:
	ROHIT	RH			
	DRAFTED BY:	CLIENT NAME:			
rohit	Yuliana Chongbang				

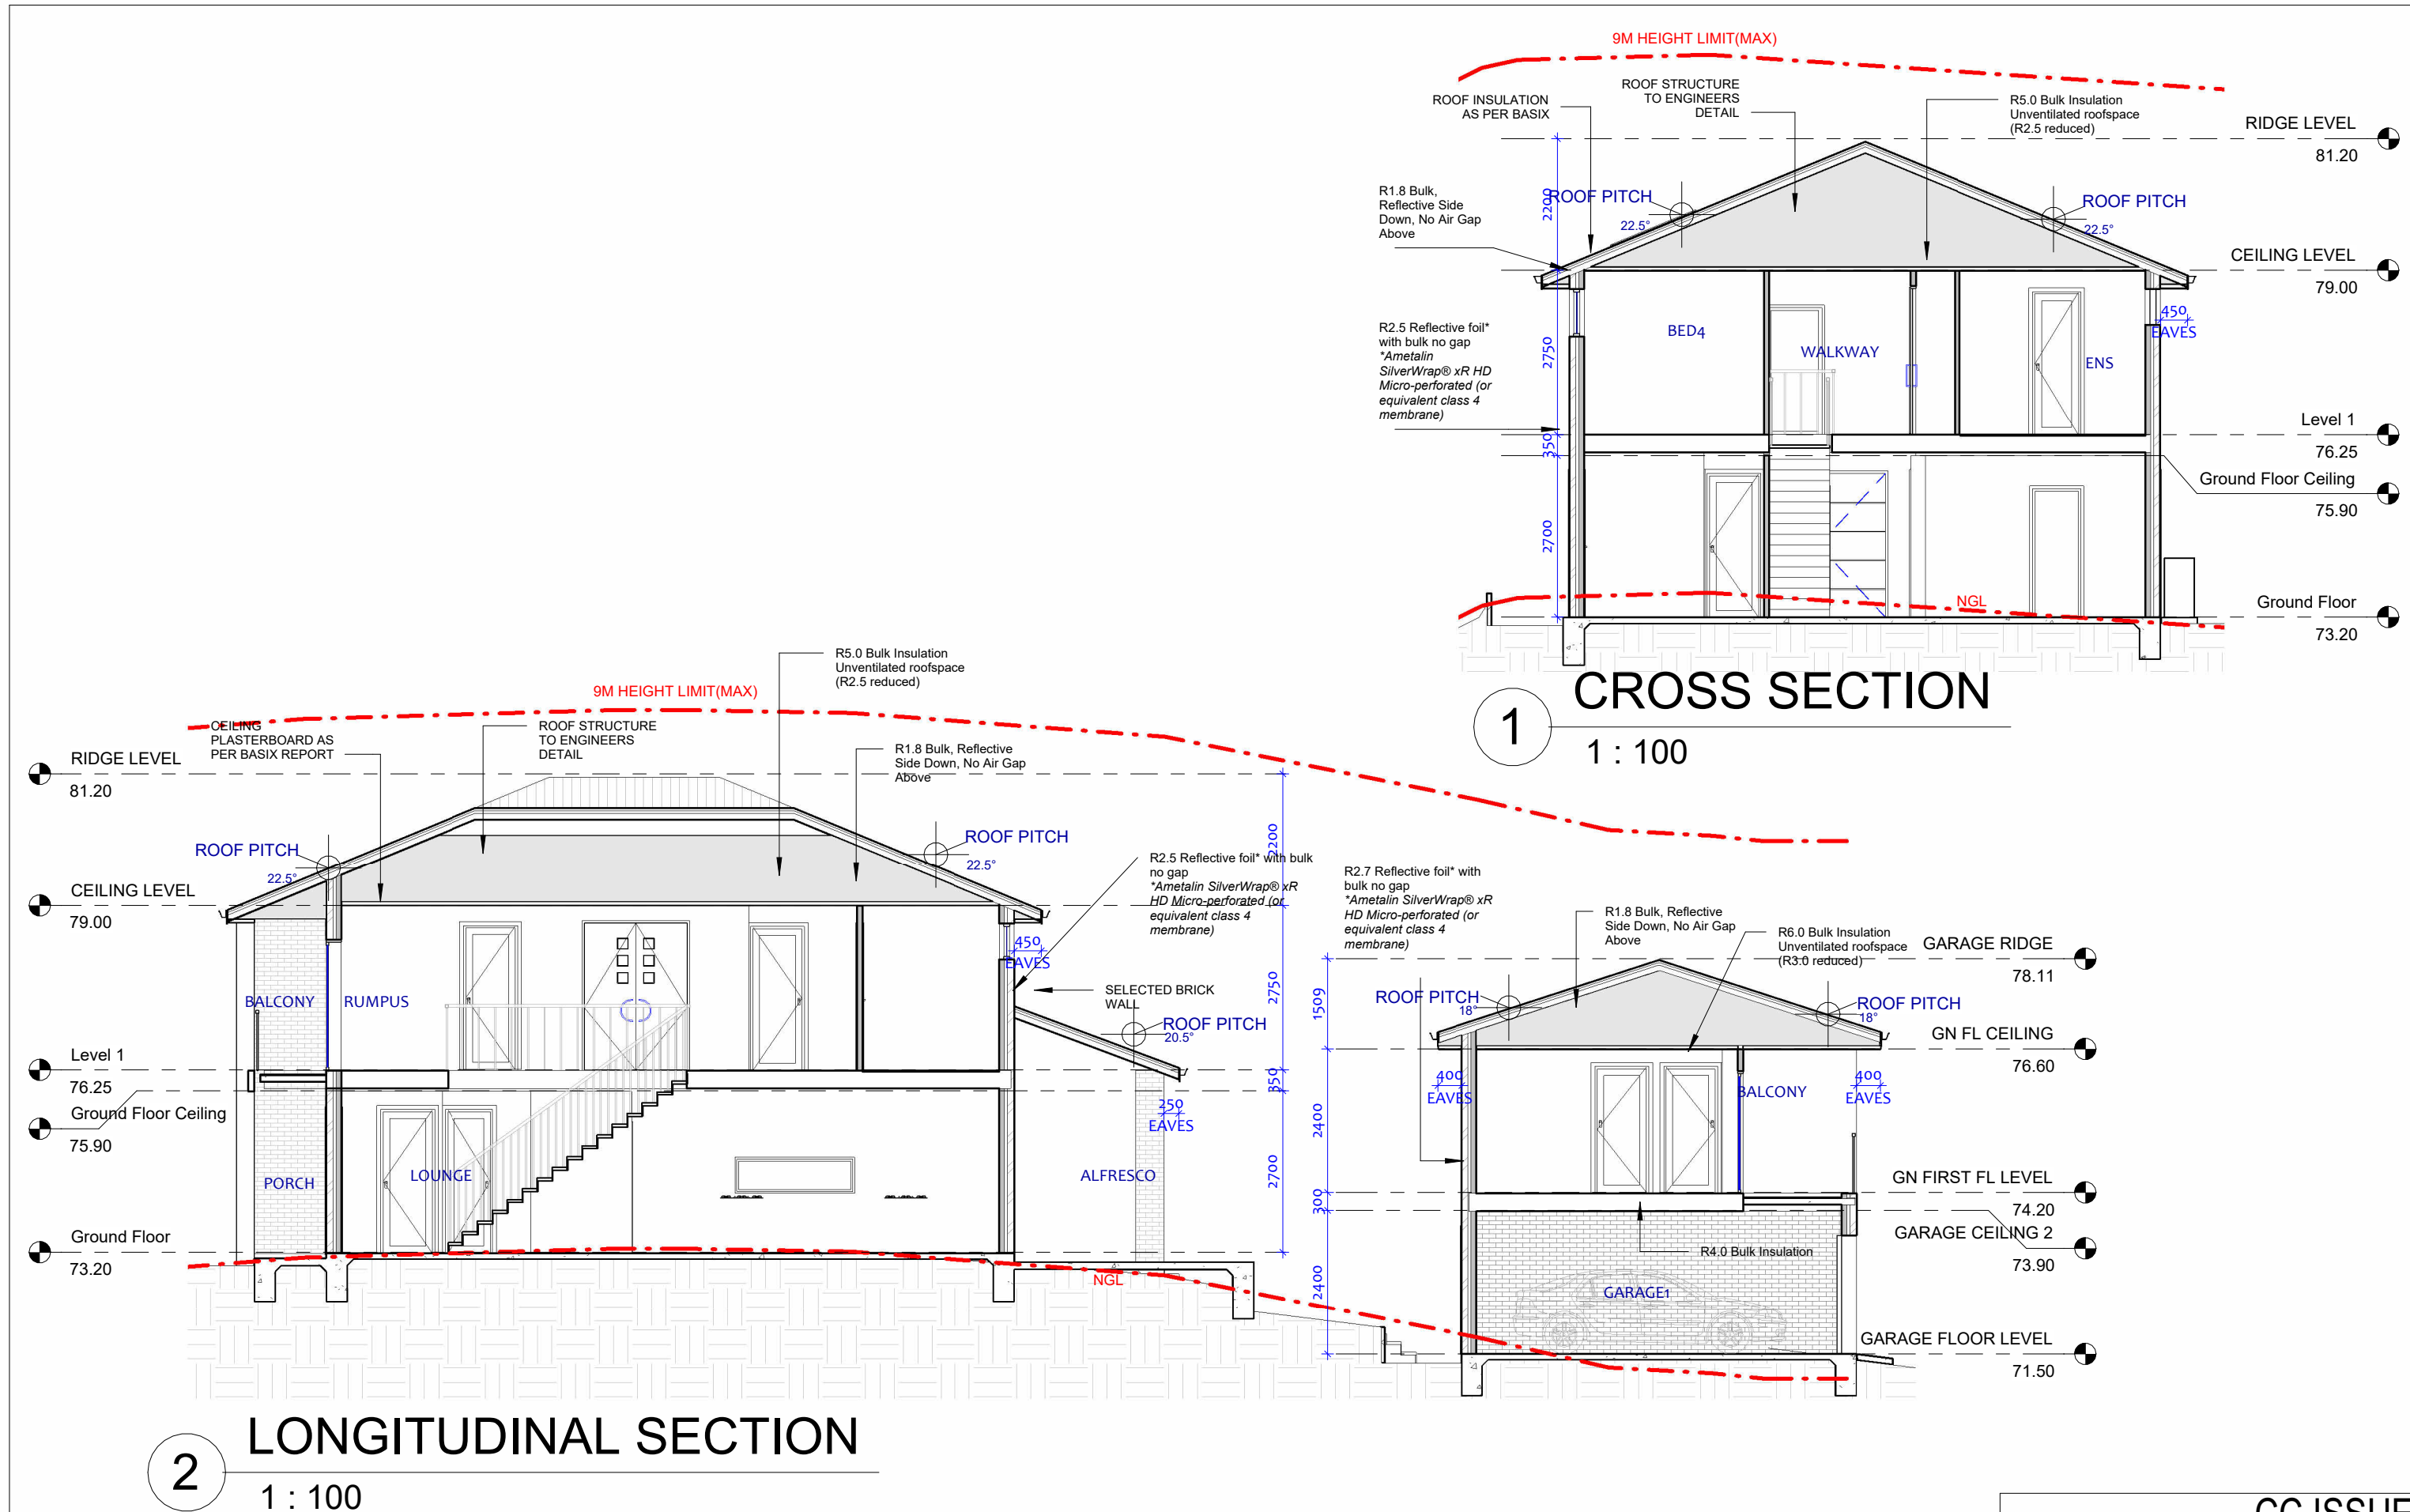

REV	DATE	DESCRIPTION	BY
2	24-07-2026	DA MOD	
1	03-02-2026	DA ISSUE	

RUBY HOMES

THIS DRAWING IS THE EXCLUSIVE PROPERTY OF THE DEVELOPER & THE REPRODUCTION OF ANY PART WITHOUT THE PRIOR WRITTEN CONSENT OF THE DEVELOPER IS A VIOLATION OF APPLICABLE LAWS. IN NO EVENT SHALL THE DEVELOPER BE HELD LIABLE FOR SPECIAL COLLATERAL, INCIDENTAL OR CONSEQUENTIAL LIABILITY IN CONNECTION WITH THE USE OF THIS DIGITAL DATA ONCE RELEASED FROM THE DEVELOPER'S OFFICE. THIS DRAWING IS TO BE READ & UNDERSTOOD IN CONJUNCTION WITH THE STRUCTURAL, MECHANICAL, ELECTRICAL & / OR ANY OTHER CONSULTANT'S DOCUMENTATION AS MAY BE APPLICABLE TO THE PROJECT PRIOR TO THE START OF ANY WORKS AND FOR ITS DURATION.

PROJECT:
LOT 2302 IN DP 1265815



161 MacDonald Rd
Bardia NSW

DRAWING TITLE:
SECTIONS

NORTH:

LOT NO:	DATE:	SCALE:	DRAWING No:	REV:
2302	1-10-2026	1 : 100	CC.10	2
DRAWN BY:	CHECKED BY:			ISSUED BY:
ROHIT	RH			
DRAFTED BY:	CLIENT NAME:			
rohit	Yuliana Chongbang			

CC ISSUE

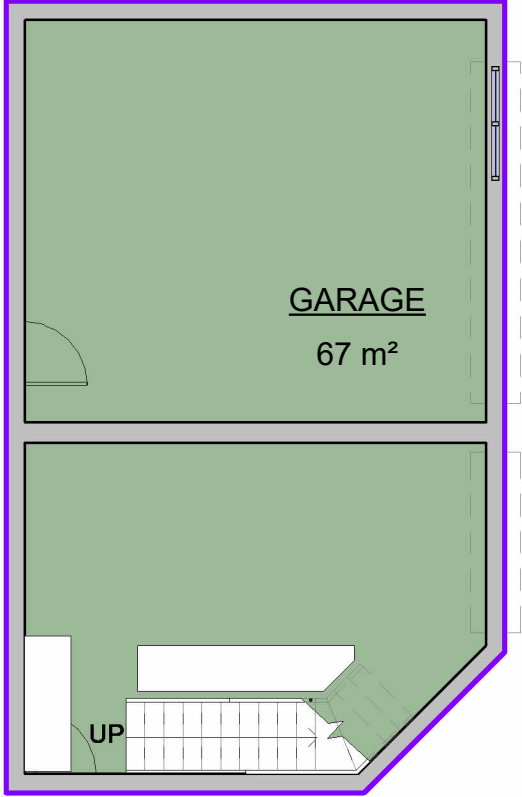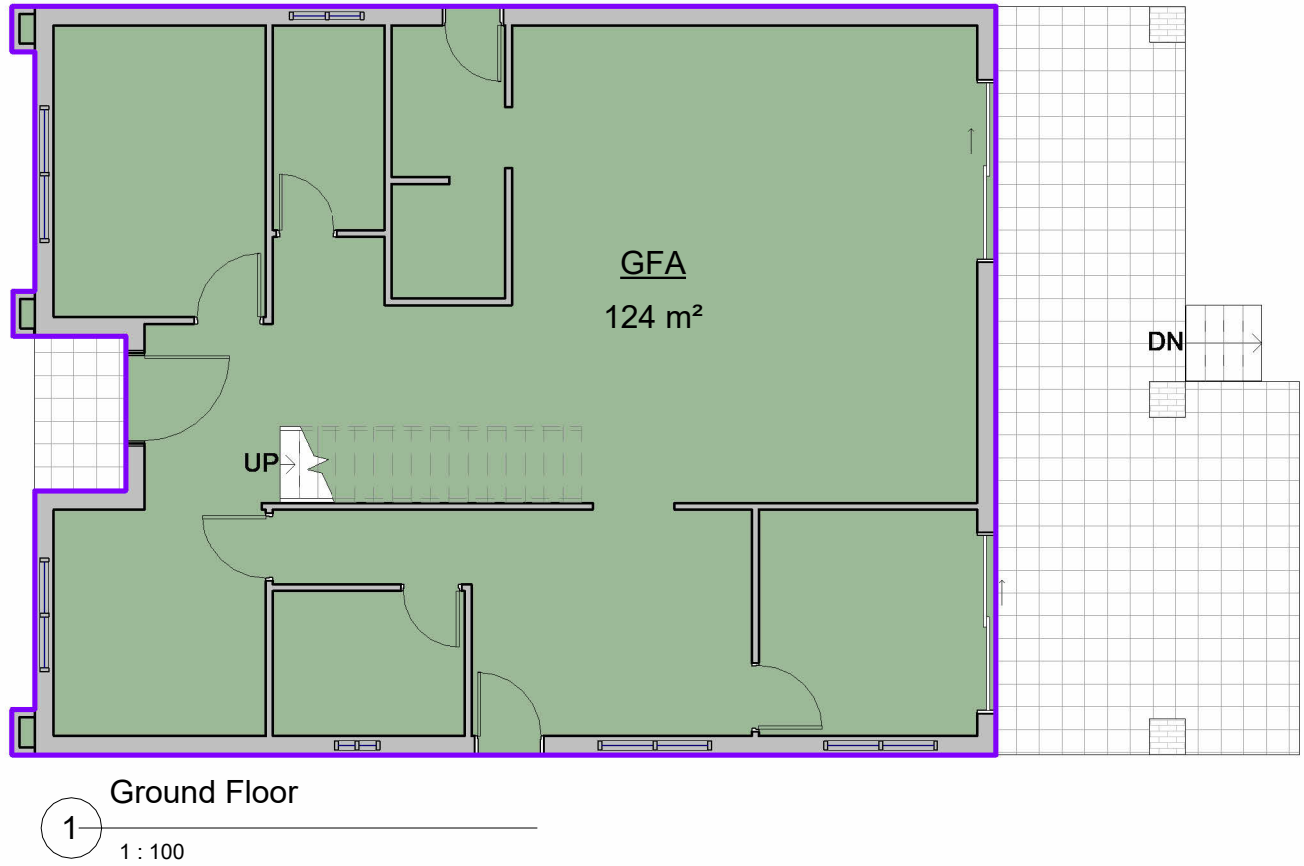

Area Schedule (Gross Building)...	
Name	Area

Ground Floor	
GFA	124 m²
GARAGE	67 m²
Ground Floor: 2	191 m²
Grand total: 2	191 m²

REV	DATE	DESCRIPTION	BY
2	24-07-2026	DA MOD	
1	03-02-2026	DA ISSUE	




THIS DRAWING IS THE EXCLUSIVE PROPERTY OF THE DEVELOPER & THE REPRODUCTION OF ANY PART WITHOUT THE PRIOR WRITTEN CONSENT OF THE DEVELOPER IS A VIOLATION OF APPLICABLE LAWS. IN NO EVENT SHALL THE DEVELOPER BE HELD LIABLE FOR SPECIAL COLLATERAL, INCIDENTAL OR CONSEQUENTIAL LIABILITY IN CONNECTION WITH THE USE OF THIS DIGITAL DATA ONCE RELEASED FROM THE DEVELOPER'S OFFICE. THIS DRAWING IS TO BE READ & UNDERSTOOD IN CONJUNCTION WITH THE STRUCTURAL, MECHANICAL, ELECTRICAL & / OR ANY OTHER CONSULTANT'S DOCUMENTATION AS MAY BE APPLICABLE TO THE PROJECT PRIOR TO THE START OF ANY WORKS AND FOR ITS DURATION.



PROJECT:
LOT 2302 IN DP 1265815

161 MacDonald Rd
Bardia NSW

DRAWING TITLE:
**COVERAGE AREA
CALCULATION**


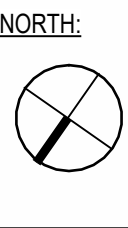


LOT NO: 2302	DATE: 1-10-2026	SCALE: 1 : 100	DRAWING No: CC.11A	REV: 2
DRAWN BY: ROHIT	CHECKED BY: RH		ISSUED BY:	
DRAFTED BY: SL	CLIENT NAME: Yuliana Chongbang			

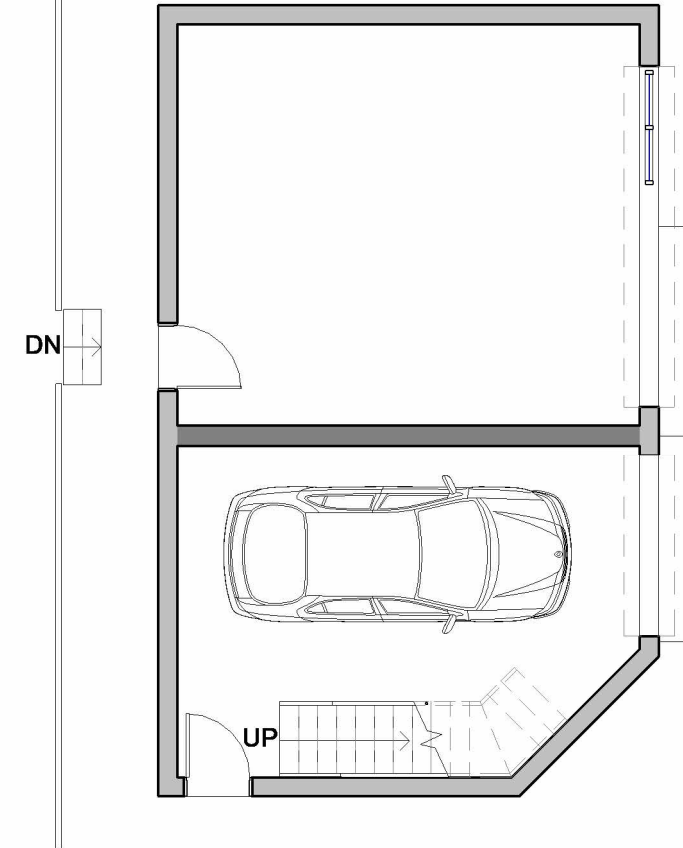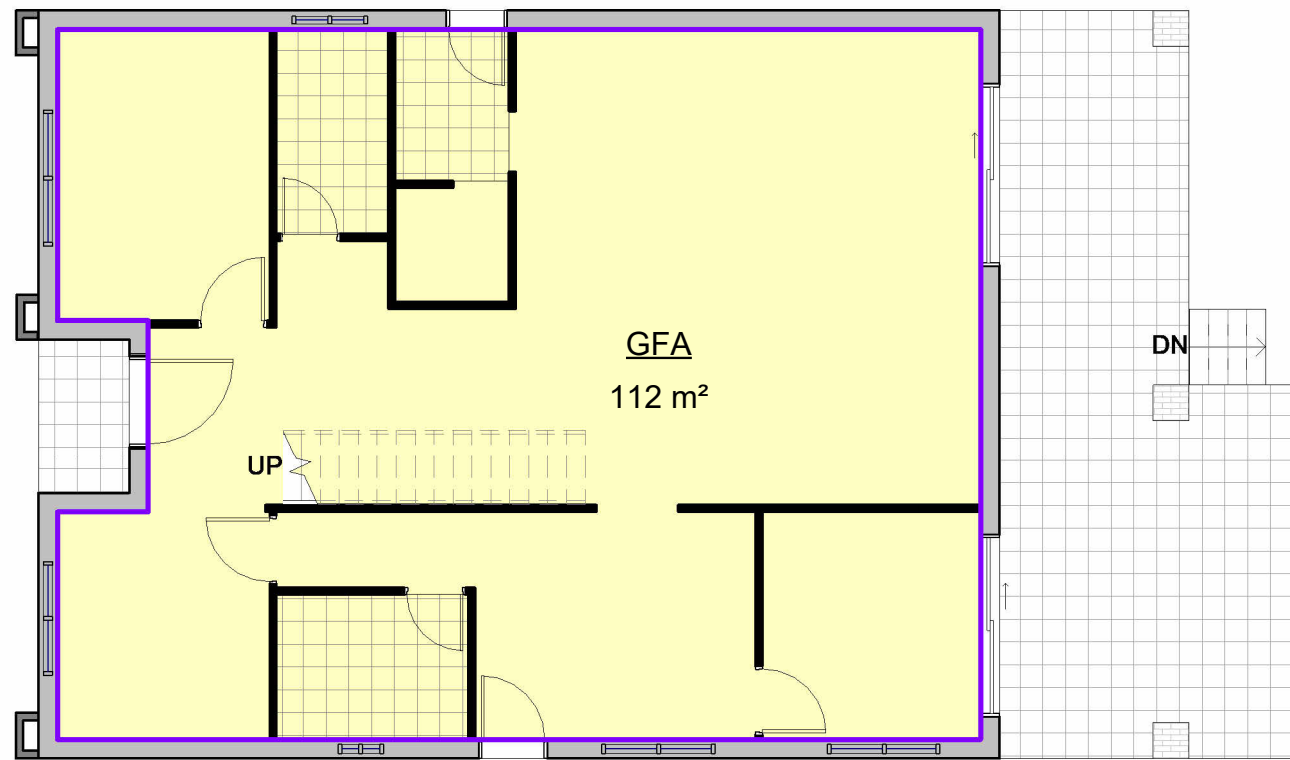

Area Schedule (Rentable)	
Name	Area
Ground Floor	
GFA	112 m ²
Ground Floor: 1	112 m ²
Level 1	
FFA	104 m ²
STUDIO	49 m ²
Level 1: 2	153 m ²
Grand total: 3	265 m ²

1 Ground Floor
1 : 100

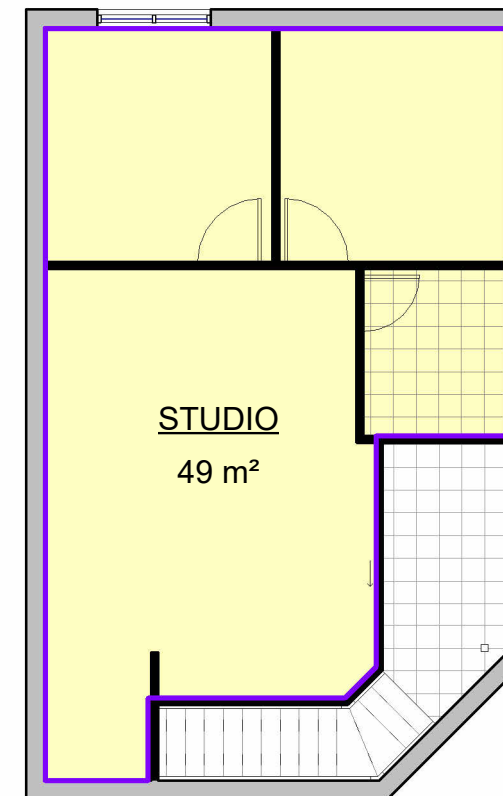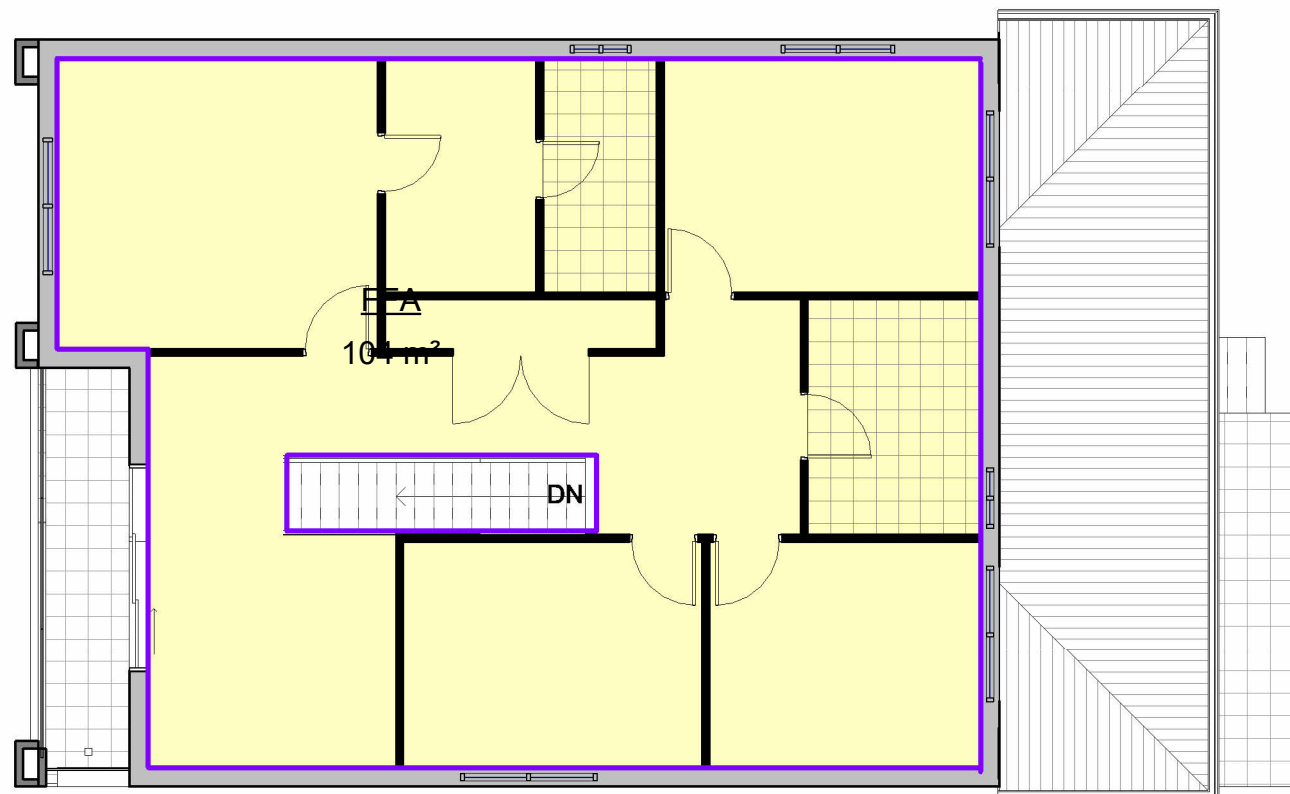

2 Level 1
1 : 100

REV	DATE	DESCRIPTION	BY
2	24-07-2026	DA MOD	
1	03-02-2026	DA ISSUE	




THIS DRAWING IS THE EXCLUSIVE PROPERTY OF THE DEVELOPER & THE REPRODUCTION OF ANY PART WITHOUT THE PRIOR WRITTEN CONSENT OF THE DEVELOPER IS A VIOLATION OF APPLICABLE LAWS. IN NO EVENT SHALL THE DEVELOPER BE HELD LIABLE FOR SPECIAL COLLATERAL, INCIDENTAL OR CONSEQUENTIAL LIABILITY IN CONNECTION WITH THE USE OF THIS DIGITAL DATA ONCE RELEASED FROM THE DEVELOPER'S OFFICE. THIS DRAWING IS TO BE READ & UNDERSTOOD IN CONJUNCTION WITH THE STRUCTURAL, MECHANICAL, ELECTRICAL & / OR ANY OTHER CONSULTANT'S DOCUMENTATION AS MAY BE APPLICABLE TO THE PROJECT PRIOR TO THE START OF ANY WORKS AND FOR ITS DURATION.



PROJECT:
LOT 2302 IN DP 1265815

161 MacDonald Rd
Bardia NSW

DRAWING TITLE:
**AREA PLAN
CALCULATION**

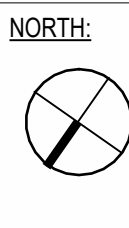

LOT NO: 2302	DATE: 1-10-2026	SCALE: 1 : 100	DRAWING No: CC.11	REV: 2
DRAWN BY: ROHIT	CHECKED BY: RH		ISSUED BY:	
DRAFTED BY: rohit	CLIENT NAME: Yuliana Chongbang			

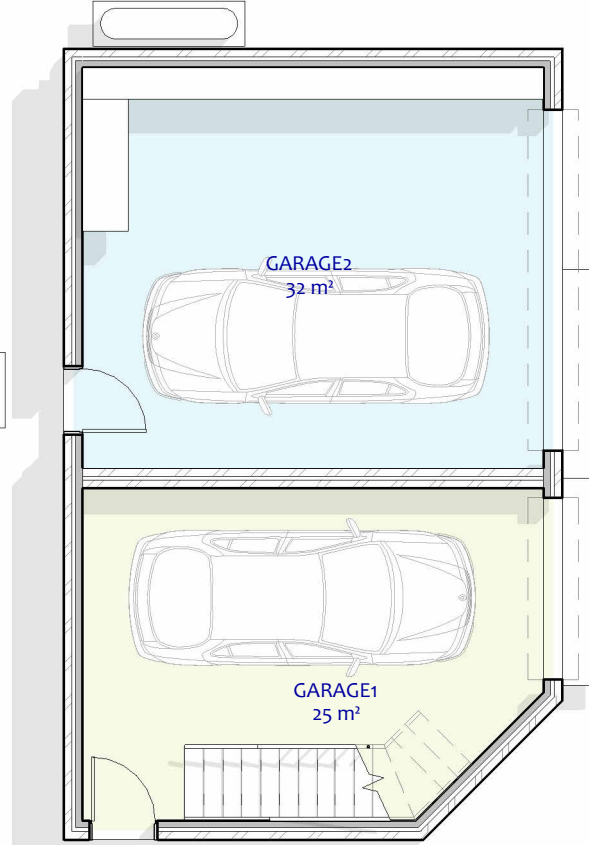
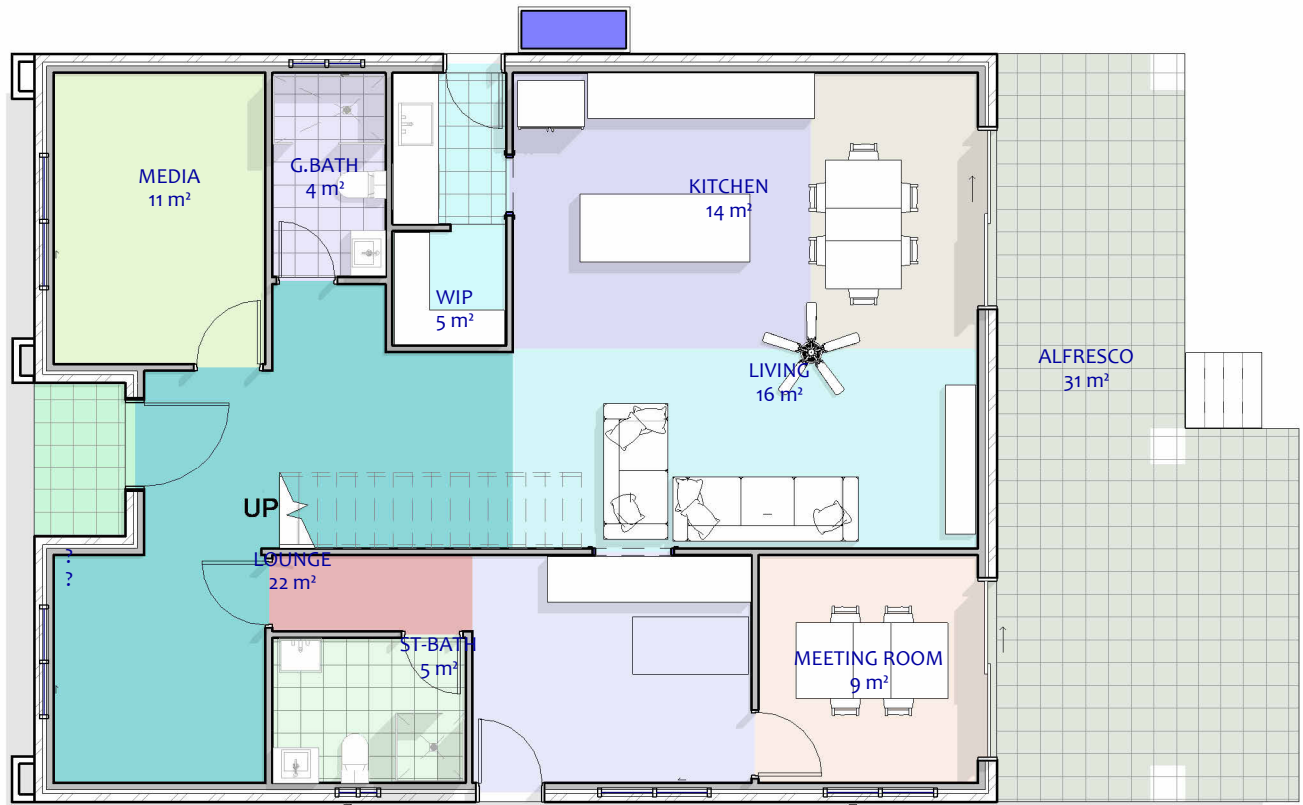


Room Schedule	
Name	Area
ALFRESCO	31 m ²
DINING	8 m ²
G.BATH	4 m ²
GARAGE1	25 m ²
GARAGE2	32 m ²
HOME OFFICE	11 m ²
KITCHEN	14 m ²
LIVING	16 m ²
LOUNGE	22 m ²
MEDIA	11 m ²
MEETING ROOM	9 m ²
PORCH	2 m ²
ST-BATH	5 m ²
WALKWAY	3 m ²
WIP	5 m ²
Ground Floor: 15	200 m ²

Room Schedule	
Name	Area
BALCONY	9 m ²
GN-BATH	4 m ²
L'DRY	3 m ²
GN FIRST FL LEVEL: 3	16 m ²
BALCONY	6 m ²
BATH	7 m ²
BED2	13 m ²
BED3	11 m ²
BED4	12 m ²
ENS	5 m ²
GN.BED1	9 m ²
GN.BED2	9 m ²
LINEN	2 m ²
M.BED	16 m ²
RUMPUS	15 m ²
WALKWAY	17 m ²
WIR	6 m ²
Level 1: 13	129 m ²
Grand total: 31	345 m ²

Ground Floor Room Area Plan

1
1 : 100

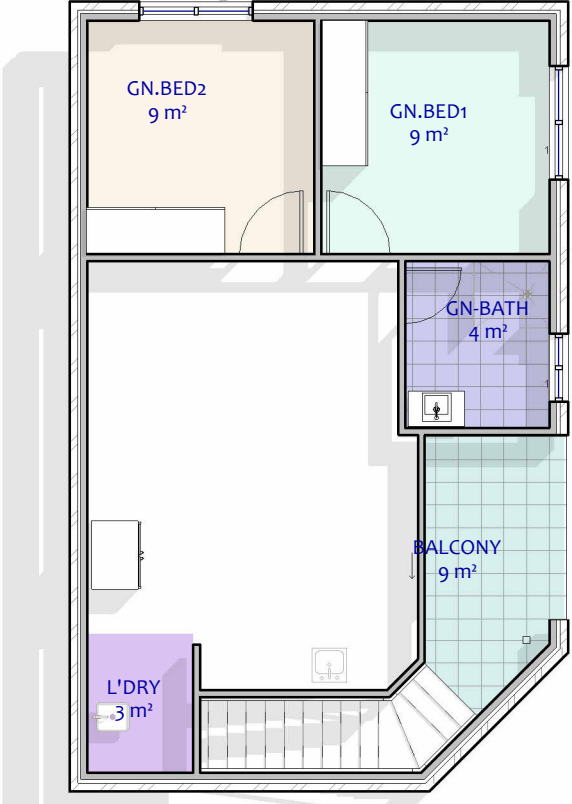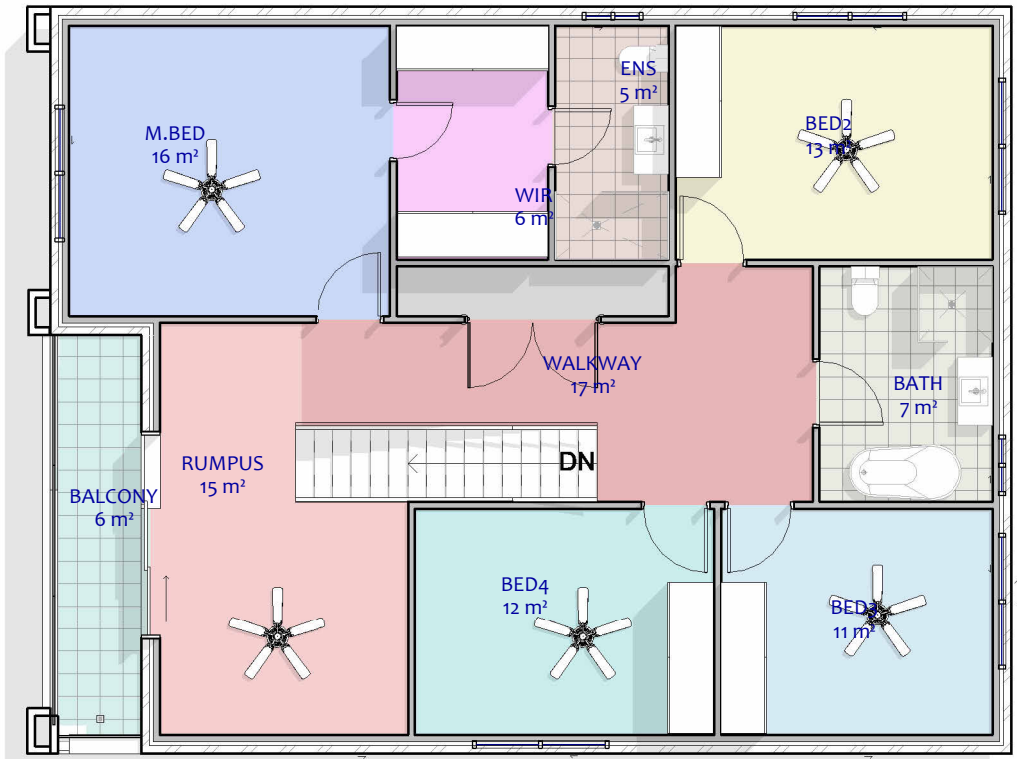

Level 1 Room Area Plan

2
1 : 100

REV	DATE	DESCRIPTION	BY
2	24-07-2026	DA MOD	
1	03-02-2026	DA ISSUE	




THIS DRAWING IS THE EXCLUSIVE PROPERTY OF THE DEVELOPER & THE REPRODUCTION OF ANY PART WITHOUT THE PRIOR WRITTEN CONSENT OF THE DEVELOPER IS A VIOLATION OF APPLICABLE LAWS. IN NO EVENT SHALL THE DEVELOPER BE HELD LIABLE FOR SPECIAL COLLATERAL, INCIDENTAL OR CONSEQUENTIAL LIABILITY IN CONNECTION WITH THE USE OF THIS DIGITAL DATA ONCE RELEASED FROM THE DEVELOPER'S OFFICE. THIS DRAWING IS TO BE READ & UNDERSTOOD IN CONJUNCTION WITH THE STRUCTURAL, MECHANICAL, ELECTRICAL & / OR ANY OTHER CONSULTANT'S DOCUMENTATION AS MAY BE APPLICABLE TO THE PROJECT PRIOR TO THE START OF ANY WORKS AND FOR ITS DURATION.

PROJECT:
LOT 2302 IN DP 1265815

161 MacDonald Rd
Bardia NSW

DRAWING TITLE:
ROOM AREA PLAN

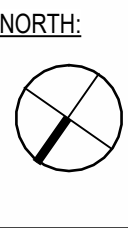

LOT NO: 2302	DATE: 1-10-2026	SCALE: 1 : 100	DRAWING No: CC.12	REV: 2
DRAWN BY: ROHIT	CHECKED BY: RH	CLIENT NAME: Yuliana Chongbang	ISSUED BY:	
DRAFTED BY: rohit				

CC ISSUE



1 FRONT FACADE



2 REAR FACADE(GARAGE GRANNY)


	1. RF	2. BR1	3. CD1	4. CR1	5. AL	6. ED	7. GD	8. FAS	9. GUT
	ROOF	MAIN WALLS	CLADDING	ACCENT 1/RENDER	WINDOWS/ BALUSTRADE	MAIN DOOR	GARAGE DOOR	FASCIA	GUTTER
MATERIAL	COLORBOND DARK MONUMENT	BRICK	BLUEBOARD	BRICK	ALUMINIUM	TIMBER	COLORBOND	COLORBOND	COLORBOND
COLOUR									

NOTE: ALL COLOURS SPECIFIED ARE INDICATIVE ONLY AND ARE SUBJECT TO VARIATION AND TO AVAILABILITY
ANY DISCREPANCY PLEASE FOLLOW AS PER RENDERED IMAGE

				CC ISSUE								
				 THIS DRAWING IS THE EXCLUSIVE PROPERTY OF THE DEVELOPER & THE REPRODUCTION OF ANY PART WITHOUT THE PRIOR WRITTEN CONSENT OF THE DEVELOPER IS A VIOLATION OF APPLICABLE LAWS. IN NO EVENT SHALL THE DEVELOPER BE HELD LIABLE FOR SPECIAL COLLATERAL, INCIDENTAL OR CONSEQUENTIAL LIABILITY IN CONNECTION WITH THE USE OF THIS DIGITAL DATA ONCE RELEASED FROM THE DEVELOPER'S OFFICE. THIS DRAWING IS TO BE READ & UNDERSTOOD IN CONJUNCTION WITH THE STRUCTURAL, MECHANICAL, ELECTRICAL & / OR ANY OTHER CONSULTANTS' DOCUMENTATION AS MAY BE APPLICABLE TO THE PROJECT PRIOR TO THE START OF ANY WORKS AND FOR ITS DURATION.	PROJECT: LOT 2302 IN DP 1265815 161 MacDonald Rd Bardia NSW	DRAWING TITLE: COLOR SCHEDULE	NORTH:	LOT NO: 2302	DATE: 1-10-2026	SCALE: 1 : 100	DRAWING No: CC.13	REV: 2
					DRAWN BY: ROHIT	CHECKED BY: RH		ISSUED BY:				
2	24-07-2026	DA MOD										
1	03-02-2026	DA ISSUE										
REV	DATE	DESCRIPTION	BY							DRAFTED BY: rohit	CLIENT NAME: Yuliana Chongbang	



THIS DRAWING IS THE EXCLUSIVE PROPERTY OF THE DEVELOPER & THE REPRODUCTION OF ANY PART WITHOUT THE PRIOR WRITTEN CONSENT OF THE DEVELOPER IS A VIOLATION OF APPLICABLE LAWS. IN NO EVENT SHALL THE DEVELOPER BE HELD LIABLE FOR SPECIAL COLLATERAL, INCIDENTAL OR CONSEQUENTIAL LIABILITY IN CONNECTION WITH THE USE OF THIS DIGITAL DATA ONCE RELEASED FROM THE DEVELOPER'S OFFICE. THIS DRAWING IS TO BE READ & UNDERSTOOD IN CONJUNCTION WITH THE STRUCTURAL, MECHANICAL, ELECTRICAL & / OR ANY OTHER CONSULTANT'S DOCUMENTATION AS MAY BE APPLICABLE TO THE PROJECT PRIOR TO THE START OF ANY WORKS AND FOR ITS DURATION.

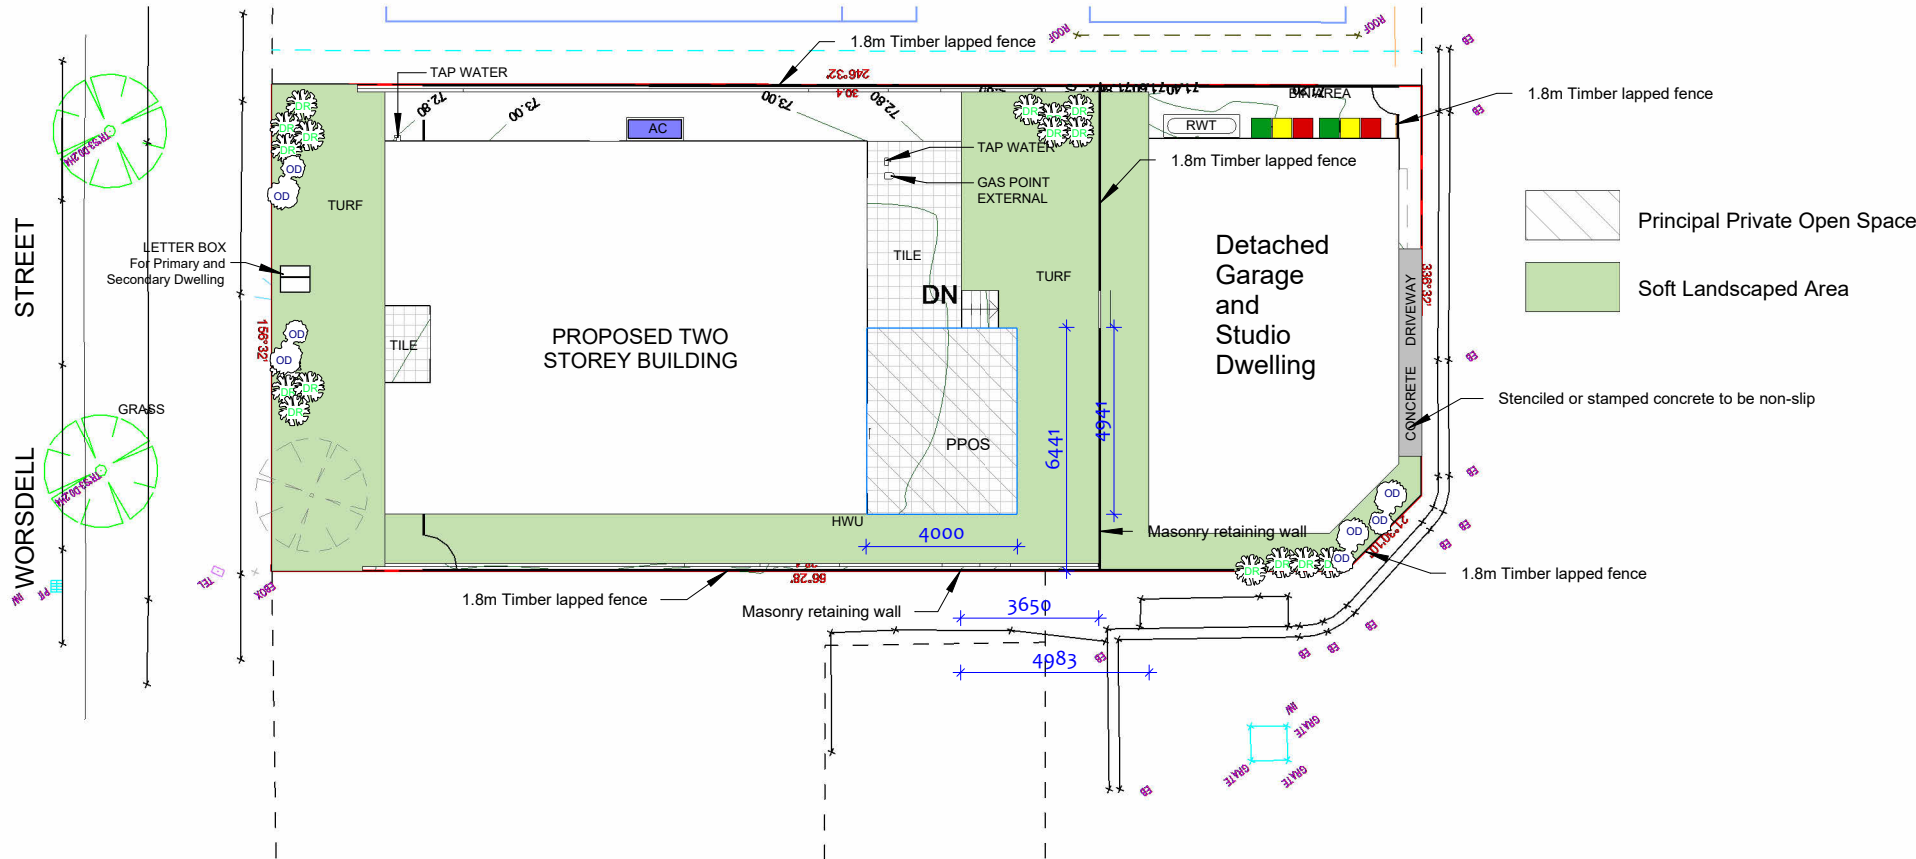

LANDSCAPE AREA	
FRONT AREA	38.5 m ²
BACKYARD AREA	90 m ²

LEGENDS	
	PROPOSED SCREENING PLANTING
	PROPOSED SHRUB PLANTING
	PROPOSED ACCENT PLANTING
	PROPOSED TREE
	PROPOSED TURF AREA TO BE SIR WALTER SOFT LEAF BUFFALO
	PROPOSED CONCRETE PATH

GENERAL NOTES:

- LANDSCAPE CONTRACTOR TO CHECK DA CONDITIONS AND STAMPED LANDSCAPE PLAN
- BEFORE COMMENCING WORKS TO ENSURE NO ADDITIONS/AMENDMENTS TO PLAN
- GARDEN BEDS IN OSD BASIN TO CONSIST OF NON FLOATABLE DECORATIVE GRAVEL.
- REFER TO HYDRAULICS ENGINEERS PLAN FOR OSD DETAILS/FINAL LEVELS.
- MULCHED PLANTING BEDS TO BE A MINIMUM DEPTH OF 75mm AS SELECTED.
- CONTRACTOR'S RESPONSIBILITY TO CHECK AND ADJUST SOIL pH AS REQUIRED.
- PROVIDE TIMBER EDGE AS A MINIMUM BENEATH FENCING/GATES TO DEFINE TURF AND GARDEN BEDS/PATHWAYS,EDGING TO BE PROVIDED TO ALL AREAS WHERE DIFFERING MATERIALS MEET i.e TURF/GARDEN,TURF/GRAVEL PATH ETC.
- WEED MAT BENEATH GRAVEL GRAVEL PATHWAYS REQUIRED TO LIMIT MUD TRACKING.
- PREMIUM ORGANIC GARDEN MIX TO BE USED.
- ALL PLANTS TO BE HEALTHY AND VIGOROUS.
- CONTRACTOR TO MAKE GOOD TURF ON NATURE STRIP POST CONSTRUCTION
- CONTRACTOR TO MAKE GOOD TURF ON NATURE STRIP POST CONSTRUCTION.
- DO NOT SCALE ARCHITECTURAL SETOUT FROM LANDSCAPE DRAWING.
- EXISTING TREE SPREAD APPROXIMATE ONLY.REFER TO TREE REPORT WHEN APPLICABLE.
- SITE SURVEY PROVIDED BY OTHERS.
- BUFFALO TURF PREFERRED OVER KIKUYU.

LANDSCAPE BASIX NOTE:
THE APPLICANT MUST PLANT INDIGENEOUS OR LOW WATER USE SPECIES OF VEGETATION THROUGHOUT 15 SQM OF THE SITE.

NOTE :BUILDER RESERVES THE RIGHT NOT TO UNDERTAKE NOR SUPPLY CERTIFICATE FOR OCCUPATION CERTIFICATE.
NOTE : TO AID COMPLIANCE WITH BASIX LEGISLATION,PLANTS (WHERE APPLICABLE) HAVE BEEN SELECTED FROM THE LOCAL CITY COUNCIL/SHIRE PLANT LISTS.
NOTE: LOCATION OF SEWER MAINS/LINES,WATER PIPES,UNDERGROUND ELECTRICITY AND OTHER SERVICES MUST BE OBTAINED PRIOR TO COMMENCEMENT OF ANY WORK ON SITE.

CONTRACTORS NOTE : CALCULATED ARES DETERMINED BY CAD AND HAVE BEEN ROUNDED UP FOR USE AS A GUIDE ONLY ALLOW STANDARD PERCENTAGE FOR CUTTING AND WASTAGE .CONFIRM DIMENSIONS AND NUMBERS PRIOR TO QUOTING/ORDERING.

LANDSCAPE PLAN

1 : 200


PLANT SCHEDULE

Genus	Common Name	Qty	Pot size	Height	width
Trees					
Backhousia myrtifolia	Grey Myrtle	1	45L	6-10m	Dense feature tree with, green glossy foliage. Greenish yellow flowers in small terminal clusters.
Shrubs					
Bursaria Spinosa Var Sppinosa	Blackthorn ,Boxthorn	8	140mm	1.5m	Thorny, wiry branches. Leaf size and shape varies with age. Small, white fragrant flowers.
Dodonea Visco ssp. Cuneata	Wedge-Leaft Hop Bush	6	140mm	1m	Compact growth. Sticky leaves taper to sharp point. Green fruit turns red and purple
Indigofera Australis	Native Indigo	5	140mm	1m	Slender, erect. Pink to lilac pea flowers, numerous along stems.
Hedgeing & screening Plants					
Acmena smithii 'Cherry Surprise'	Lilly Pilly Cherry Surprise PBR	10	140mm	3m	It has attractive small dense green foliage that provides a continuous flush of cherry-red new growth nearly all year round. Small white starry flowers bloom in summer.




Backhousia myrtifolia
Grey Myrtle

Type: Tree. *Description:* Dense feature tree with, green glossy foliage. Greenish yellow flowers in small terminal clusters. *Height:* 6-10m. *Flowers:* Nov-Dec. *Propagation:* sow seed in Spring. *Prune:* minimally.

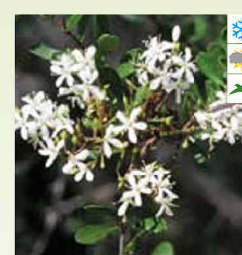


Bursaria spinosa
var spinosa
Blackthorn, Boxthorn

Type: Shrub. *Description:* Thorny, wiry branches. Leaf size and shape varies with age. Small, white fragrant flowers. *Height:* Medium. *Flowers:* Jan-April. *Propagation:* sow seed. *Prune:* after flowering, only to maintain shape.

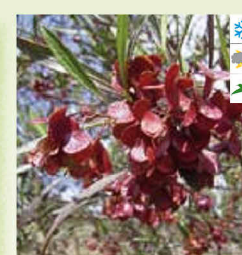

Dodonaea viscosa ssp. cuneata
Wedge-leaf Hop Bush

Type: Shrub. *Description:* Compact growth. Sticky leaves taper to sharp point. Green fruit turns red and purple. *Height:* 1m. *Flowers:* Spring. *Propagation:* sow from seed or take cutting in Spring and Summer. *Prune:* minimally.

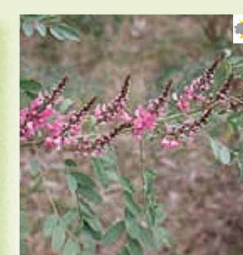

Indigofera australis
Native Indigo

Type: Shrub. *Description:* Slender, erect. Pink to lilac pea flowers, numerous along stems. *Height:* 1m Alluvial Aug-Sept. *Flowers:* Spring. *Propagation:* from cutting, early to mid Summer. *Prune:* trim lightly after flowering.


REV	DATE	DESCRIPTION	BY
2	24-07-2026	DA MOD	
1	03-02-2026	DA ISSUE	

THIS DRAWING IS THE EXCLUSIVE PROPERTY OF THE DEVELOPER & THE REPRODUCTION OF ANY PART WITHOUT THE PRIOR WRITTEN CONSENT OF THE DEVELOPER IS A VIOLATION OF APPLICABLE LAWS. IN NO EVENT SHALL THE DEVELOPER BE HELD LIABLE FOR SPECIAL COLLATERAL, INCIDENTAL OR CONSEQUENTIAL LIABILITY IN CONNECTION WITH THE USE OF THIS DIGITAL DATA ONCE RELEASED FROM THE DEVELOPER'S OFFICE. THIS DRAWING IS TO BE READ & UNDERSTOOD IN CONJUNCTION WITH THE STRUCTURAL, MECHANICAL, ELECTRICAL & / OR ANY OTHER CONSULTANT'S DOCUMENTATION AS MAY BE APPLICABLE TO THE PROJECT PRIOR TO THE START OF ANY WORKS AND FOR ITS DURATION.

PROJECT:
LOT 2302 IN DP 1265815

161 MacDonald Rd
Bardia NSW

DRAWING TITLE:
LANDSCAPE PLAN

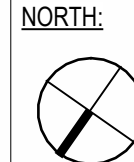

LOT NO: 2302	DATE: 1-10-2026	SCALE: 1 : 200	DRAWING No: CC.14	REV: 2
DRAWN BY: ROHIT	CHECKED BY: RH			ISSUED BY:
DRAFTED BY: rohit	CLIENT NAME: Yuliana Chongbang			

Nationwide House Energy Rating Scheme®
NatHERS® Certificate No. 0012381463-02

Generated on 11 Aug 2026 using BERS Pro v5.2.6 (3.23)

Property

Address Unit Main Dw, 161 Macdonald Road,
Bardia , NSW , 2565
Lot/DP Lot 2302 DP 1265815
NCC class* 1a
Floor/all Floors G of 2 floors
Type New Home

Plans

Main plan n/a
Prepared by n/a

Construction and environment

Assessed floor area [m²]*
Conditioned* 198.2
Unconditioned* 16.9
Total 215.2
Garage 0.0
Exposure type Suburban
NatHERS climate zone 28 Richmond



Name Zoran Cvetkovski
Business name Sustainability-Z
Email sustainability-z@outlook.com
Phone 0414273176
Accreditation No. DMN/13/1641
Assessor Accrediting Organisation Design Matters National
Declaration of interest Declaration not completed


NCC Requirements

NCC provisions Volume Two
State/Territory variation Yes

National Construction Code (NCC) requirements

The NCC allows the use of NatHERS accredited software to comply with the energy efficiency requirements for houses (Class 1 buildings) and apartments (Class 2 sole-occupancy units and Class 4 parts of buildings). The applicable requirements for houses are detailed in Specification 42 of NCC Volume Two. For apartments the requirements are detailed in clauses J3D3 and J3D15 of NCC Volume One.
The NCC, and associated ABCB Standards and support material, can be accessed at www.abcb.gov.au.
Note, variations and additions to the NCC energy efficiency requirements may apply in some states and territories.

Thermal performance
star rating

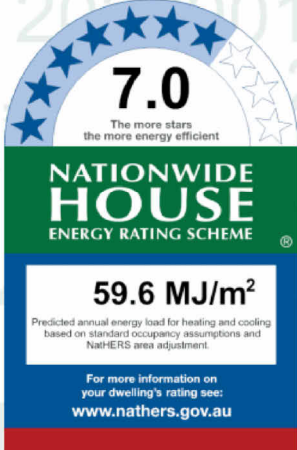

Thermal performance [MJ/m²]

Limits taken from ABCB Standard 2022
Area adjustment included

	Heating	Cooling
Modelled	36.8	22.9
Load limits	N/A	N/A

Features determining load limits
Floor Type (lowest conditioned area) CSOG
NCC climate zone 1 or 2 No
Outdoor living area No
Outdoor living area ceiling fan No

Whole of Home
performance rating

No Whole of Home
performance rating
generated for this
certificate.

Verification

To verify this certificate,
scan the QR code or visit
hstar.com.au/QR/Generate?p=uNwFHEzsl
When using either link,
ensure you are visiting
hstar.com.au



Version 2025.0
* Refer to glossary
Generated on 11 Aug 2026 using BERS Pro v5.2.6 (3.23) for Unit Main Dw, 161 Macdonald Road , Bardia , NSW , 2565

Page 1 of 16

Nationwide House Energy Rating Scheme®
NatHERS® Certificate No. 0012381455-04

Generated on 11 Aug 2026 using BERS Pro v5.2.6 (3.23)

Property

Address Unit Sec Dw, 161 Macdonald Road,
Bardia , NSW , 2565
Lot/DP Lot 2302 DP 1265815
NCC class* 1a
Floor/all Floors G of 2 floors
Type New Home

Plans

Main plan n/a
Prepared by n/a

Construction and environment

Assessed floor area [m²]*
Conditioned* 44.4
Unconditioned* 4.1
Total 81.4
Garage 32.9
Exposure type Suburban
NatHERS climate zone 28 Richmond



Name Zoran Cvetkovski
Business name Sustainability-Z
Email sustainability-z@outlook.com
Phone 0414273176
Accreditation No. DMN/13/1641
Assessor Accrediting Organisation Design Matters National
Declaration of interest Declaration not completed


NCC Requirements

NCC provisions Volume Two
State/Territory variation Yes

National Construction Code (NCC) requirements

The NCC allows the use of NatHERS accredited software to comply with the energy efficiency requirements for houses (Class 1 buildings) and apartments (Class 2 sole-occupancy units and Class 4 parts of buildings). The applicable requirements for houses are detailed in Specification 42 of NCC Volume Two. For apartments the requirements are detailed in clauses J3D3 and J3D15 of NCC Volume One.
The NCC, and associated ABCB Standards and support material, can be accessed at www.abcb.gov.au.
Note, variations and additions to the NCC energy efficiency requirements may apply in some states and territories.

Thermal performance
star rating

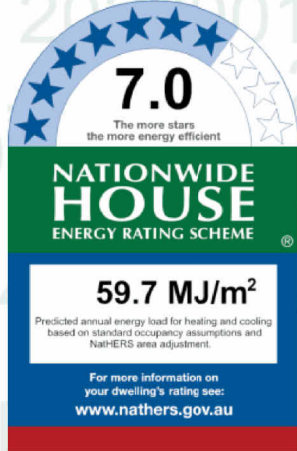

Thermal performance [MJ/m²]

Limits taken from ABCB Standard 2022
Area adjustment included

	Heating	Cooling
Modelled	30.1	29.6
Load limits	N/A	N/A

Features determining load limits
Floor Type (lowest conditioned area) CSOG
NCC climate zone 1 or 2 No
Outdoor living area No
Outdoor living area ceiling fan No

Whole of Home
performance rating

No Whole of Home
performance rating
generated for this
certificate.

Verification

To verify this certificate,
scan the QR code or visit
hstar.com.au/QR/Generate?p=SxLkLcSe
When using either link,
ensure you are visiting
hstar.com.au



Version 2025.0
* Refer to glossary
Generated on 11 Aug 2026 using BERS Pro v5.2.6 (3.23) for Unit Sec Dw, 161 Macdonald Road , Bardia , NSW , 2565

Page 1 of 11

Nationwide House Energy Rating Scheme®
Multiple Class 1 dwellings Summary
NatHERS® Certificate No. 0012381470

Generated on 11 Aug 2026 using BERS Pro v5.2.6 (3.23)

Property

Address 161 Macdonald Road,
Bardia , NSW , 2565
Lot/DP Lot 2302 DP 1265815
NatHERS Climate Zone 28 Richmond



Name Zoran Cvetkovski
Business name Sustainability-Z
Email sustainability-z@outlook.com
Phone 0414273176
Accreditation No. DMN/13/1641
Assessor Accrediting Organisation Design Matters National

Verification

To verify this certificate, scan the
QR code or visit
hstar.com.au/QR/Generate?p=VzLozhAgU
When using either link, ensure
you are visiting hstar.com.au



National Construction Code (NCC) requirements

The NCC allows the use of NatHERS accredited software to comply with the energy efficiency requirements for houses (Class 1 buildings) and apartments (Class 2 sole-occupancy units and Class 4 parts of buildings). The applicable requirements for houses are detailed in Specification 42 of NCC Volume Two. For apartments the requirements are detailed in clauses J3D3 and J3D15 of NCC Volume One.
The NCC, and associated ABCB Standards and support material, can be accessed at www.abcb.gov.au.
Note, variations and additions to the NCC energy efficiency requirements may apply in some states and territories.

Summary of all dwellings

Certificate number and link	Unit Number	Heating load (load limit) [MJ/m²/p.a.]	Cooling load (load limit) [MJ/m²/p.a.]	Total load [MJ/m²/p.a.]	Star Rating	Whole of Home Rating
0012381463-02	Main Dw	36.8 (N/A)	22.9 (N/A)	59.6	7	0
0012381455-04	Sec Dw	30.1 (N/A)	29.6 (N/A)	59.7	7	0

Version 2025.0
Nationwide House Energy Rating Scheme (NatHERS) is an initiative of the Australian, state and territory governments. For more details see www.nathers.gov.au
Generated on 11 Aug 2026 using BERS Pro v5.2.6 (3.23) for 161 Macdonald Road , Bardia , NSW , 2565

Page 1 of 2

				CC ISSUE			
				DATE:	SCALE:	DRAWING No:	REV:
				1-10-2026		CC.15	2
				CHECKED BY:			ISSUED BY:
				RH			
				DRAFTED BY:	CLIENT NAME:		
				rohit	Yuliana Chongbang		
2	24-07-2026	DA MOD					
1	03-02-2026	DA ISSUE					
REV	DATE	DESCRIPTION	BY				



THIS DRAWING IS THE EXCLUSIVE PROPERTY OF THE DEVELOPER & THE REPRODUCTION OF ANY PART WITHOUT THE PRIOR WRITTEN CONSENT OF THE DEVELOPER IS A VIOLATION OF APPLICABLE LAWS. IN NO EVENT SHALL THE DEVELOPER BE HELD LIABLE FOR SPECIAL COLLATERAL, INCIDENTAL OR CONSEQUENTIAL LIABILITY IN CONNECTION WITH THE USE OF THIS DIGITAL DATA ONCE RELEASED FROM THE DEVELOPER'S OFFICE. THIS DRAWING IS TO BE READ & UNDERSTOOD IN CONJUNCTION WITH THE STRUCTURAL, MECHANICAL, ELECTRICAL & / OR ANY OTHER CONSULTANT'S DOCUMENTATION AS MAY BE APPLICABLE TO THE PROJECT PRIOR TO THE START OF ANY WORKS AND FOR ITS DURATION.

PROJECT:
LOT 2302 IN DP 1265815

161 MacDonald Rd
Bardia NSW

DRAWING TITLE:
BASIX

NORTH:

LOT NO:

2302

DRAWN BY:

ROHIT

DRAFTED BY:

rohit

DATE:

1-10-2026

CHECKED BY:

RH

CLIENT NAME:

Yuliana Chongbang

CC ISSUE

DRAWING No:

CC.15

REV:

2

ISSUED BY:

/For details: See the Basix certificate/

The applicant must install a Central rainwater tank of at least 2000 litres.

The rainwater tank to collect rain runoff from at least 100 m² of the roof /See the central systems/

The applicant must connect the rainwater tank to:

- all toilets
- all laundries
- the rainwater tank to allow irrigation of min. 103 m2, common landscaping in the development /See the central systems/

- Shower heads 3 star (> 7.5 but <= 9.0 L/min)
- Toilets.....4 star
- Kitchen tap.....5 star
- Basin Taps.....5 star

Hot Water System: Gas instantaneous with a performance of 6 stars (Main Dwelling)

Hot Water System: Gas instantaneous with a performance of 6 stars (Secondary Dwelling)

Heating/Cooling: 3-phase air-conditioning; Energy rating: EER 2.5-3.0 (Zoned) (Main Dwelling)

Heating/Cooling: 1-phase air-conditioning: Energy rating: 3* Average zone (Living ONLY) (Secondary Dwelling)

Ventilation (Main Dwelling): Bathrooms (individual fan, ducted; operation: interlocked to light with timer off), Kitchen (individual fan, ducted; operation: manual on/off) & Laundry (individual fan, ducted; operation: interlocked to light).

Ventilation (Sec. Dwelling): Bathroom (no mechanical ventilation; natural), Kitchen (individual fan, ducted; operation: manual on/off) & Laundry (individual fan, ducted; operation: interlocked to light).

Natural lighting: Window/skylight in the Kitchen and 4 Bathrooms/Toilets (Main Dwelling)

Natural lighting: Window/skylight in 1 Bathroom/Toilet (Sec. Dwelling)

Artificial lighting (For Each Dwelling):

- The applicant must ensure that a minimum of 80% of light fixtures are fitted with fluorescent, compact fluorescent, or light-emitting-diode (LED) lamps.

- The applicant must install a gas cooktop & electric oven in the kitchen of each dwelling
- The applicant must install fixed outdoor clothes drying line for each dwelling.

- The applicant must install a photovoltaic system as part of the development. The applicant must connect this system to the development's electrical system.
- The photovoltaic system must consist of photovoltaic collectors with the capacity to generate at least 1 peak kilowatts of electricity, installed at an angle between 10 degrees and 25 degrees to the horizontal facing northwest.

The Basix certificate should be read in conjunction with the Nathers certificate (including the additional notes pages 4 & 5).

/For Details: see the Nathers certificate

A detailed method of assessment with greater flexibility of solution choice and capacity to assess complex dwelling designs.

The dwelling design has been assessed with NatHERS software from an accredited assessor

- Timber Stud Frame Brick Veneer, R2.7 Reflective foil* with bulk no gap (Main Dwelling)
- Timber Stud Frame Brick Veneer, R2.7 Reflective foil* with bulk no gap (Sec. Dwelling)
- Fibro Timber Stud Frame Panel on Battens, R2.7 Anti-glare foil with bulk no gap (Sec. Dwelling)

**Ametalin SilverWrap® xR HD Micro-perforated (or equivalent class 4 membrane)*

- Timber Stud Frame, Direct Fix Plasterboard, R 2.7 Bulk Insulation, No Air Gap (Sec. Dwelling-against Bath)
- Timber Stud Frame, Direct Fix Plasterboard, No Insulation (All Others)

- Concrete Slab on Ground
- Suspended Floor Timber Frame, R 5.0 Bulk Insulation (Sec Dw)

- Timber Framed Timber Above Plasterboard, R4.0 Bulk Insulation (Above Garage-Main Dw)
- Timber Framed Timber Above Plasterboard, R5.0 Bulk Insulation (Above Garage-Sec Dw)
- Timber Framed Timber Above Plasterboard, No Insulation (All Others)

- Plasterboard on Timber, R2.5 Bulk Insulation Unventilated roofspace (Main Dwelling -Reduced insulation near the eave in the distance of 580mm)
- Plasterboard on Timber, R5.0 Bulk Insulation Unventilated roofspace (Main Dwelling -All others/unaffected ceiling area)
- Plasterboard on Timber, R3.0 Bulk Insulation Unventilated roofspace (Sec. Dwelling -Reduced insulation near the eave in the distance of 580mm)
- Plasterboard on Timber, R6.0 Bulk Insulation Unventilated roofspace (Sec. Dwelling -All others/unaffected ceiling area)

- Waterproofing Membrane, No Insulation, Only an Air Gap
- Corrugated Iron Timber Frame, R1.8 Bulk, Reflective Side Down, No Air Gap Above

Note: All coffer ceiling verticals and walls against the roof-space, to be insulated, with the same insulation as the ceiling insulation

Note: All downlights: IC-F /IC-4/ (insulation covered/ including the control gears/) rated as per AS/NZS standard 60598 and IP (sealed) rated as per BS EN 60529:1992, European IEC 60509:1989

Note: (where the roof is extended over an open area such as a deck or carport): A barrier to be installed within the roof space to separate the space above the zoned part of the house and the space above the open veranda.

The building fabric, including insulation and air cavity ventilation, must meet the requirements specified in Part H Energy Efficiency (Volume 2) of the NCC and the ABCB Housing Provisions 10.8 and 13.2. These standards are essential to ensure proper energy efficiency and compliance in construction practices.

Note-Ceiling fans: For the number and the location, see the Nathers certificate

				CC ISSUE									
				 THIS DRAWING IS THE EXCLUSIVE PROPERTY OF THE DEVELOPER & THE REPRODUCTION OF ANY PART WITHOUT THE PRIOR WRITTEN CONSENT OF THE DEVELOPER IS A VIOLATION OF APPLICABLE LAWS. IN NO EVENT SHALL THE DEVELOPER BE HELD LIABLE FOR SPECIAL COLLATERAL, INCIDENTAL OR CONSEQUENTIAL LIABILITY IN CONNECTION WITH THE USE OF THIS DIGITAL DATA ONCE RELEASED FROM THE DEVELOPER'S OFFICE. THIS DRAWING IS TO BE READ & UNDERSTOOD IN CONJUNCTION WITH THE STRUCTURAL, MECHANICAL, ELECTRICAL & / OR ANY OTHER CONSULTANT'S DOCUMENTATION AS MAY BE APPLICABLE TO THE PROJECT PRIOR TO THE START OF ANY WORKS AND FOR ITS DURATION.	PROJECT: LOT 2302 IN DP 1265815 161 MacDonald Rd Bardia NSW	DRAWING TITLE: BASIX 01	NORTH:	LOT NO: 2302	DATE: 1-10-2026	SCALE:	DRAWING No: CC.15a	REV: 2	
												CHECKED BY: RH	ISSUED BY:
2	24-07-2026	DA MOD									DRAWN BY: ROHIT	CLIENT NAME: Yuliana Chongbang	
1	03-02-2026	DA ISSUE											
REV	DATE	DESCRIPTION	BY										

Window Schedule 1					
Mark	Height	Width	Sill Height	Head Height	Description

Ground Floor

GNW6	1500	600	900	2400	SLIDING
GW1	1800	1500	600	2400	SLIDING
GW2	1800	1800	600	2400	SLIDING
GW3	600	1000	1800	2400	SLIDING
GW4	600	2000	1000	1600	FIXED
GW6	1500	1500	900	2400	SLIDING
GW7	1500	1500	900	2400	SLIDING

Ground Floor: 7

GN FIRST FL LEVEL

GNW1	600	1500	1800	2400	SLIDING
GNW2	1250	1500	1150	2400	SLIDING
GNW3	600	900	1800	2400	SLIDING

GN FIRST FL LEVEL: 3

Level 1

FW1	1800	1803	650	2450	SLIDING
FW2	600	800	1850	2450	SLIDING
FW3	600	1500	1850	2450	SLIDING
FW4	1000	1800	1450	2450	SLIDING
FW5	1000	1800	1450	2450	SLIDING
FW6	800	1800	1650	2450	SLIDING
GNW4	600	800	1850	2450	SLIDING

Level 1: 7

Door Schedule 1				
Mark	Height	Width	Count	Description

GARAGE FLOOR LEVEL

D6	2040	820	1	FLUSH DOOR
D7	2040	820	1	FLUSH DOOR
GD1	2000	2400	1	GARAGE DOOR
GD2	2000	4500	1	GARAGE DOOR

GARAGE FLOOR LEVEL: 4

Ground Floor

D1	2340	820	1	FLUSH DOOR
D2	2340	720	1	FLUSH DOOR
D3	2340	720	1	FLUSH DOOR
D4	2340	820	1	FLUSH DOOR
D5	2340	820	1	FLUSH DOOR
D8	2340	720	1	FLUSH DOOR
D9	2340	820	1	FLUSH DOOR
MD	2400	1120	1	SOLID CORE DOOR
SD1	2300	2400	1	SLIDING DOOR
SD9	2300	2400	1	SLIDING DOOR

Ground Floor: 10

GN FIRST FL LEVEL

D15	2040	820	1	FLUSH DOOR
D16	2040	820	1	FLUSH DOOR
D17	2040	720	1	FLUSH DOOR
SD3	2000	2000	1	SLIDING DOOR

GN FIRST FL LEVEL: 4

Level 1

D10	2340	720	1	FLUSH DOOR
D11	2500	1800	1	FLUSH DOOR
D12	2340	820	1	FLUSH DOOR
D13	2340	820	1	FLUSH DOOR
D14	2340	820	1	FLUSH DOOR
D18	2340	820	1	FLUSH DOOR
D19	2340	720	1	FLUSH DOOR
D20	2340	820	1	FLUSH DOOR
SD2	2140	2650	1	SLIDING DOOR

Level 1: 9

				CC ISSUE								
				 THIS DRAWING IS THE EXCLUSIVE PROPERTY OF THE DEVELOPER & THE REPRODUCTION OF ANY PART WITHOUT THE PRIOR WRITTEN CONSENT OF THE DEVELOPER IS A VIOLATION OF APPLICABLE LAWS. IN NO EVENT SHALL THE DEVELOPER BE HELD LIABLE FOR SPECIAL COLLATERAL, INCIDENTAL OR CONSEQUENTIAL LIABILITY IN CONNECTION WITH THE USE OF THIS DIGITAL DATA ONCE RELEASED FROM THE DEVELOPER'S OFFICE. THIS DRAWING IS TO BE READ & UNDERSTOOD IN CONJUNCTION WITH THE STRUCTURAL, MECHANICAL, ELECTRICAL & / OR ANY OTHER CONSULTANT'S DOCUMENTATION AS MAY BE APPLICABLE TO THE PROJECT PRIOR TO THE START OF ANY WORKS AND FOR ITS DURATION.	PROJECT: LOT 2302 IN DP 1265815 161 MacDonald Rd Bardia NSW	DRAWING TITLE: DOOR/ WINDOW SCHEDULE	NORTH:	LOT NO:	DATE:	SCALE:	DRAWING No:	REV:
2	24-07-2026	DA MOD										2302
1	03-02-2026	DA ISSUE						DRAWN BY:	CHECKED BY:			
REV	DATE	DESCRIPTION	BY					ROHIT	RH			
								DRAFTED BY:	CLIENT NAME:			
								rohit	Yuliana Chongbang			



THIS DRAWING IS THE EXCLUSIVE PROPERTY OF THE DEVELOPER & THE REPRODUCTION OF ANY PART WITHOUT THE PRIOR WRITTEN CONSENT OF THE DEVELOPER IS A VIOLATION OF APPLICABLE LAWS. IN NO EVENT SHALL THE DEVELOPER BE HELD LIABLE FOR SPECIAL COLLATERAL, INCIDENTAL OR CONSEQUENTIAL LIABILITY IN CONNECTION WITH THE USE OF THIS DIGITAL DATA ONCE RELEASED FROM THE DEVELOPER'S OFFICE. THIS DRAWING IS TO BE READ & UNDERSTOOD IN CONJUNCTION WITH THE STRUCTURAL, MECHANICAL, ELECTRICAL & / OR ANY OTHER CONSULTANT'S DOCUMENTATION AS MAY BE APPLICABLE TO THE PROJECT PRIOR TO THE START OF ANY WORKS AND FOR ITS DURATION.

PROJECT:

LOT 2302 IN DP 1265815

161 MacDonald Rd
Bardia NSW

DRAWING TITLE:

DOOR/ WINDOW SCHEDULE

NORTH:

LOT NO:
2302

DRAWN BY:
ROHIT

DRAFTED BY:
rohit

DATE:
1-10-2026

CHECKED BY:
RH


CLIENT NAME:
Yuliana Chongbang

SCALE:


DRAWING No:
CC.18

REV:
2

ISSUED BY:

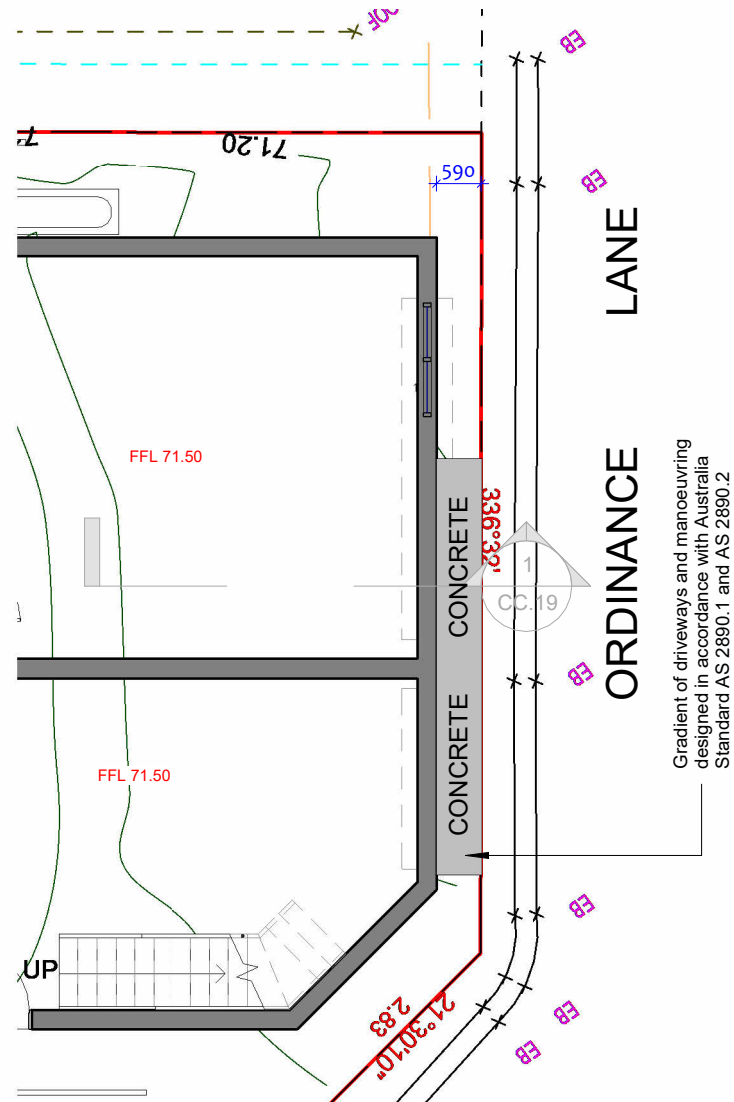

3 CC - DRIVEWAY PLAN
1 : 100

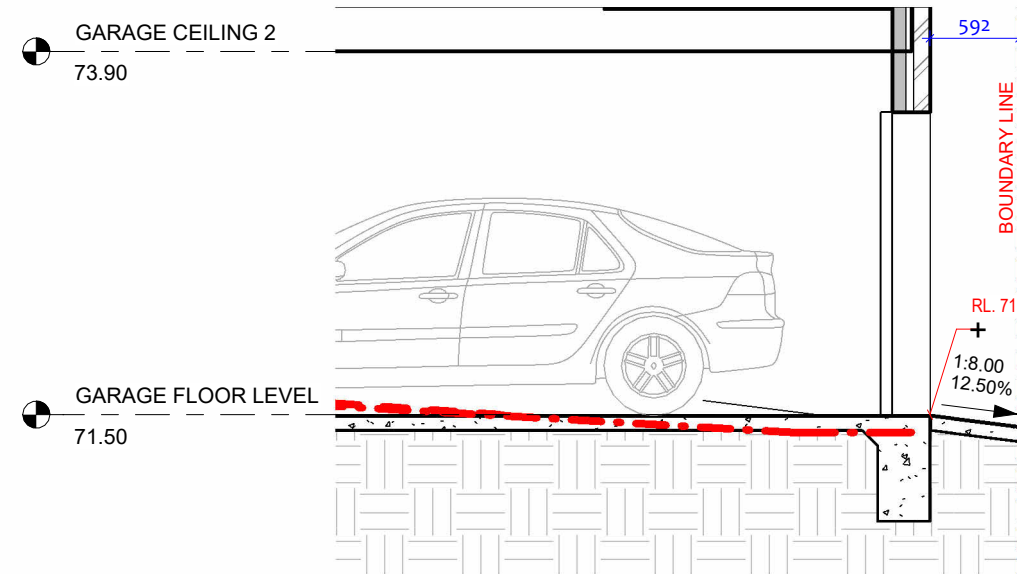

1 DRIVEWAY SECTION
1 : 50

				CC ISSUE			
REV	DATE	DESCRIPTION	BY	LOT NO:	DATE:	SCALE:	DRAWING No:
				2302	1-10-2026	As indicated	CC.19
				DRAWN BY:	CHECKED BY:		REV:
2	24-07-2026	DA MOD		ROHIT	RH		2
1	03-02-2026	DA ISSUE					ISSUED BY:
				DRAFTED BY:	CLIENT NAME:		
				rohit	Yuliana Chongbang		

THIS DRAWING IS THE EXCLUSIVE PROPERTY OF THE DEVELOPER & THE REPRODUCTION OF ANY PART WITHOUT THE PRIOR WRITTEN CONSENT OF THE DEVELOPER IS A VIOLATION OF APPLICABLE LAWS. IN NO EVENT SHALL THE DEVELOPER BE HELD LIABLE FOR SPECIAL COLLATERAL, INCIDENTAL OR CONSEQUENTIAL LIABILITY IN CONNECTION WITH THE USE OF THIS DIGITAL DATA ONCE RELEASED FROM THE DEVELOPER'S OFFICE. THIS DRAWING IS TO BE READ & UNDERSTOOD IN CONJUNCTION WITH THE STRUCTURAL, MECHANICAL, ELECTRICAL & / OR ANY OTHER CONSULTANT'S DOCUMENTATION AS MAY BE APPLICABLE TO THE PROJECT PRIOR TO THE START OF ANY WORKS AND FOR ITS DURATION.

PROJECT:

LOT 2302 IN DP 1265815

161 MacDonald Rd
Bardia NSW

DRAWING TITLE:

DRIVEWAY
DETAILS

NORTH: