



ECOTECH
DESIGNS

BUILDING DREAMS SUSTAINABLY



DRAWING TITLE

COVER PAGE

DRAWING NO

CC01

PROJECT

PROPOSED ATTACHED DUAL OCCUPANCY

ADDRESS

26 MARSKELL CIRCUIT MUDGEE
LOT 28 | DP 1307255

BASIX Commitments

Basix Certificate No. 1794716S_02

26 MARSKELL CIRCUIT MUDGEE

BASIX™Certificate

Building Sustainability Index
www.planningportal.nsw.gov.au/development-and-assessment/basix

Single Dwelling

Certificate number: 1794716S_02

This certificate confirms that the proposed development will meet the NSW government's requirements for sustainability, if it is built in accordance with the commitments set out below. Terms used in this certificate, or in the commitments, have the meaning given by the document entitled "BASIX Definitions" dated 10/09/2020 published by the Department. This document is available at www.planningportal.nsw.gov.au/definitions

Secretary
Date of issue: Friday, 07 November 2025
To be valid, this certificate must be submitted with a development application or lodged with a complying development certificate application within 3 months of the date of issue.



WATER Commitments

Schedule of BASIX commitments

The commitments set out below regulate how the proposed development is to be carried out. It is a condition of any development consent granted, or complying development certificate issued, for the proposed development, that BASIX commitments be complied with.

Water Commitments	Show on DA plans	Show on CC/CDC plans & specs	Certifier check
Landscape			
The applicant must plant indigenous or low water use species of vegetation throughout 70 square metres of the site.	✔	✔	
Fixtures			
The applicant must install showerheads with a minimum rating of 4 star (> 4.5 but <= 6 L/min plus spray force and/or coverage tests) in all showers in the development.		✔	✔
The applicant must install a toilet flushing system with a minimum rating of 4 star in each toilet in the development.		✔	✔
The applicant must install taps with a minimum rating of 4 star in the kitchen in the development.		✔	
The applicant must install basin taps with a minimum rating of 4 star in each bathroom in the development.		✔	
Alternative water			
Rainwater tank			
The applicant must install a rainwater tank of at least 3000 litres on the site. This rainwater tank must meet, and be installed in accordance with, the requirements of all applicable regulatory authorities.	✔	✔	✔
The applicant must configure the rainwater tank to collect rain runoff from at least 185 square metres of the roof area of the development (excluding the area of the roof which drains to any stormwater tank or private dam).		✔	✔
The applicant must connect the rainwater tank to:		✔	✔
• at least one outdoor tap in the development (Note: NSW Health does not recommend that rainwater be used for human consumption in areas with potable water supply.)			

ENERGY Commitments

Energy Commitments	Show on DA plans	Show on CC/CDC plans & specs	Certifier check
Hot water			
The applicant must install the following hot water system in the development, or a system with a higher energy rating: gas instantaneous with a performance of 5.5 stars.	✔	✔	✔
Cooling system			
The applicant must install the following cooling system, or a system with a higher energy rating, in at least 1 living area: 1-phase airconditioning - ducted; Energy rating: 7 star (cold zone)		✔	✔
The applicant must install the following cooling system, or a system with a higher energy rating, in at least 1 bedroom: airconditioning ducting only; Energy rating: n/a		✔	✔
Heating system			
The applicant must install the following heating system, or a system with a higher energy rating, in at least 1 living area: 1-phase airconditioning - ducted; Energy rating: 7 star (cold zone)		✔	✔
The applicant must install the following heating system, or a system with a higher energy rating, in at least 1 bedroom: airconditioning ducting only; Energy rating: n/a		✔	✔
Ventilation			
The applicant must install the following exhaust systems in the development: At least 1 Bathroom: individual fan, ducted to façade or roof; Operation control: manual switch on/off		✔	✔
Kitchen: individual fan, ducted to façade or roof; Operation control: manual switch on/off		✔	✔
Laundry: individual fan, ducted to façade or roof; Operation control: manual switch on/off		✔	✔
Artificial lighting			
The applicant must ensure that a minimum of 80% of light fixtures are fitted with fluorescent, compact fluorescent, or light-emitting-diode (LED) lamps.		✔	✔
Natural lighting			
The applicant must install a window and/or skylight in 1 bathroom(s)/toilet(s) in the development for natural lighting.	✔	✔	✔
Other			
The applicant must install a gas cooktop & electric oven in the kitchen of the dwelling.		✔	
The applicant must install a fixed outdoor clothes drying line as part of the development.		✔	

THERMAL Commitments

Thermal Performance and Materials commitments	Show on DA plans	Show on CC/CDC plans & specs	Certifier check
Do-it-yourself Method			
General features			
The dwelling must be a Class 1 dwelling according to the National Construction Code, and must not have more than 2 storeys.	✔	✔	✔
The conditioned floor area of the dwelling must not exceed 300 square metres.	✔	✔	✔
The dwelling must not contain open mezzanine area exceeding 25 square metres.	✔	✔	✔
The dwelling must not contain third level habitable attic room.		✔	✔
Floor, walls and ceiling/roof			
The applicant must construct the floor(s), walls, and ceiling/roof of the dwelling in accordance with the specifications listed in the table below.	✔	✔	✔
The applicant must adopt one of the options listed in the tables below to address thermal bridging in metal framed floor(s), walls and ceiling/roof of the dwelling.	✔	✔	✔
The applicant must show through receipts that the materials purchased for construction are consistent with the specifications listed in the tables below.			✔

Construction	Area - m²	Additional insulation required	Options to address thermal bridging	Other specifications
floor - concrete slab on ground, waffle pod slab	120	nil/not specified	nil	
garage floor - concrete slab on ground, waffle pod slab	18	none	nil	
external wall: brick veneer; frame: timber - H2 treated softwood	all external walls	2.94 (or 3.50 including construction)/fireglass batts or roll + reflective foil in the cavity	nil	wall colour: Light (solar absorptance < 0.48)
internal wall: plasterboard; frame: timber - H2 treated softwood	80	none	nil	

Construction	Area - m²	Additional insulation required	Options to address thermal bridging	Other specifications
ceiling and roof - flat ceiling / pitched roof, framed - metal roof, timber - H2 treated softwood	175	ceiling: 4.5 (up), roof: foil backed blanket ceiling; foil backed blanket; roof: foil backed blanket.	nil	roof space ventilation: unventilated; roof colour: medium (solar absorptance 0.6-0.7); ceiling area fully insulated

Note	• Insulation specified in this Certificate must be installed in accordance with the ABCB Housing Provisions (Part 13.2.2) of the National Construction Code.
Note	• If the additional ceiling insulation listed in the table above is greater than R3.0, refer to the ABCB Housing Provisions (Part 13.2.3 (6)) of the National Construction Code.
Note	• In some climate zones, insulation should be installed with due consideration of condensation and associated interaction with adjoining building materials.

Thermal Performance and Materials commitments	Show on DA plans	Show on CC/CDC plans & specs	Certifier check
Glazed windows, doors and skylights			
The applicant must install the windows, glazed doors and shading devices described in the table below, in accordance with the specifications listed in the table. Relevant overshadowing specifications must be satisfied for each glazed window and door.	✔	✔	✔
The dwelling may have 1 skylight (<0.7 square metres) which is not listed in the table.	✔	✔	✔
The following requirements must also be satisfied in relation to each window and glazed door:	✔	✔	✔
• The applicant must install windows and glazed doors in accordance with the height and width, frame and glazing types listed in the table.	✔	✔	✔
• Each window and glazed door must have a U-value no greater than that listed and a Solar Heat Gain Coefficient (SHGC) within the range listed. Total system U values and SHGC must be calculated in accordance with National Fenestration Rating Council (NFRC) conditions.		✔	✔
The applicant must install the skylights described in the table below, in accordance with the specifications listed in the table. Total skylight area must not exceed 3 square metres (the 3 square metre limit does not include the optional additional skylight of less than 0.7 square metres that does not have to be listed in the table).	✔	✔	✔

Skylight no.	Maximum area (m²)	Skylight specification	Shading device
S01	1.00	aluminium, single clear (U: <=7.3, SHGC: 0.75 - 0.83)	no shading
S02	1.00	aluminium, single clear (U: <=7.3, SHGC: 0.75 - 0.83)	no shading
S03	1.00	aluminium, single clear (U: <=7.3, SHGC: 0.75 - 0.83)	no shading

Glazed window/door no.	Maximum height (mm)	Maximum width (mm)	Frame and glass specification	Shading device (Dimension within 10%)	Overshadowing
East facing					
W01	1200.00	1500.00	thermally broken aluminium, single glazed (U-value: <=3.0, SHGC: >0.49)	none	not overshadowed
South facing					
W02	2100.00	1000.00	thermally broken aluminium, single glazed (U-value: <=3.0, SHGC: >0.49)	none	not overshadowed
W03	850.00	2000.00	thermally broken aluminium, single glazed (U-value: <=3.0, SHGC: >0.49)	none	not overshadowed
W04	850.00	2000.00	thermally broken aluminium, single glazed (U-value: <=3.0, SHGC: >0.49)	none	not overshadowed
W05	850.00	2000.00	thermally broken aluminium, single glazed (U-value: <=3.0, SHGC: >0.49)	none	not overshadowed
W06	650.00	1550.00	thermally broken aluminium, single glazed (U-value: <=3.0, SHGC: >0.49)	none	not overshadowed
West facing					
W07	850.00	2000.00	thermally broken aluminium, single glazed (U-value: <=3.0, SHGC: >0.49)	none	not overshadowed
D01	2400.00	3200.00	thermally broken aluminium, single glazed (U-value: <=3.0, SHGC: >0.49)	none	not overshadowed

BASIX Commitments

Basix Certificate No. 1794720S_02

26B MARSKELL CIRCUIT MUDGEE

BASIX™Certificate

Building Sustainability Index
www.planningportal.nsw.gov.au/development-and-assessment/basix

Single Dwelling

Certificate number: 1794720S_02

This certificate confirms that the proposed development will meet the NSW government's requirements for sustainability, if it is built in accordance with the commitments set out below. Terms used in this certificate, or in the commitments, have the meaning given by the document entitled "BASIX Definitions" dated 10/09/2020 published by the Department. This document is available at www.planningportal.nsw.gov.au/definitions

Secretary
Date of issue: Friday, 07 November 2025
To be valid, this certificate must be submitted with a development application or lodged with a complying development certificate application within 3 months of the date of issue.



WATER Commitments

Schedule of BASIX commitments

The commitments set out below regulate how the proposed development is to be carried out. It is a condition of any development consent granted, or complying development certificate issued, for the proposed development, that BASIX commitments be complied with.

Water Commitments	Show on DA plans	Show on CC/CDC plans & specs	Certifier check
Landscape			
The applicant must plant indigenous or low water use species of vegetation throughout 70 square metres of the site.	✔	✔	
Fixtures			
The applicant must install showerheads with a minimum rating of 4 star (> 4.5 but <= 6 L/min plus spray force and/or coverage tests) in all showers in the development.		✔	✔
The applicant must install a toilet flushing system with a minimum rating of 4 star in each toilet in the development.		✔	✔
The applicant must install taps with a minimum rating of 4 star in the kitchen in the development.		✔	
The applicant must install basin taps with a minimum rating of 4 star in each bathroom in the development.		✔	
Alternative water			
Rainwater tank			
The applicant must install a rainwater tank of at least 3000 litres on the site. This rainwater tank must meet, and be installed in accordance with, the requirements of all applicable regulatory authorities.	✔	✔	✔
The applicant must configure the rainwater tank to collect rain runoff from at least 185 square metres of the roof area of the development (excluding the area of the roof which drains to any stormwater tank or private dam).		✔	✔
The applicant must connect the rainwater tank to:		✔	✔
• at least one outdoor tap in the development (Note: NSW Health does not recommend that rainwater be used for human consumption in areas with potable water supply.)			

ENERGY Commitments

Energy Commitments	Show on DA plans	Show on CC/CDC plans & specs	Certifier check
Hot water			
The applicant must install the following hot water system in the development, or a system with a higher energy rating: gas instantaneous with a performance of 5.5 stars.	✔	✔	✔
Cooling system			
The applicant must install the following cooling system, or a system with a higher energy rating, in at least 1 living area: 1-phase airconditioning - ducted; Energy rating: 7 star (cold zone)		✔	✔
The applicant must install the following cooling system, or a system with a higher energy rating, in at least 1 bedroom: airconditioning ducting only; Energy rating: n/a		✔	✔
Heating system			
The applicant must install the following heating system, or a system with a higher energy rating, in at least 1 living area: 1-phase airconditioning - ducted; Energy rating: 7 star (cold zone)		✔	✔
The applicant must install the following heating system, or a system with a higher energy rating, in at least 1 bedroom: airconditioning ducting only; Energy rating: n/a		✔	✔
Ventilation			
The applicant must install the following exhaust systems in the development: At least 1 Bathroom: individual fan, ducted to façade or roof; Operation control: manual switch on/off		✔	✔
Kitchen: individual fan, ducted to façade or roof; Operation control: manual switch on/off		✔	✔
Laundry: individual fan, ducted to façade or roof; Operation control: manual switch on/off		✔	✔
Artificial lighting			
The applicant must ensure that a minimum of 80% of light fixtures are fitted with fluorescent, compact fluorescent, or light-emitting-diode (LED) lamps.		✔	✔
Natural lighting			
The applicant must install a window and/or skylight in 1 bathroom(s)/toilet(s) in the development for natural lighting.	✔	✔	✔
Other			
The applicant must install a gas cooktop & electric oven in the kitchen of the dwelling.		✔	
The applicant must install a fixed outdoor clothes drying line as part of the development.		✔	

THERMAL Commitments

Thermal Performance and Materials commitments	Show on DA plans	Show on CC/CDC plans & specs	Certifier check
Do-it-yourself Method			
General features			
The dwelling must be a Class 1 dwelling according to the National Construction Code, and must not have more than 2 storeys.	✔	✔	✔
The conditioned floor area of the dwelling must not exceed 300 square metres.	✔	✔	✔
The dwelling must not contain open mezzanine area exceeding 25 square metres.	✔	✔	✔
The dwelling must not contain third level habitable attic room.		✔	✔
Floor, walls and ceiling/roof			
The applicant must construct the floor(s), walls, and ceiling/roof of the dwelling in accordance with the specifications listed in the table below.	✔	✔	✔
The applicant must adopt one of the options listed in the tables below to address thermal bridging in metal framed floor(s), walls and ceiling/roof of the dwelling.	✔	✔	✔
The applicant must show through receipts that the materials purchased for construction are consistent with the specifications listed in the tables below.			✔

Construction	Area - m²	Additional insulation required	Options to address thermal bridging	Other specifications
floor - concrete slab on ground, waffle pod slab	120	nil/not specified	nil	
garage floor - concrete slab on ground, waffle pod slab	18	none	nil	
external wall: brick veneer; frame: timber - H2 treated softwood	all external walls	2.94 (or 3.50 including construction)/fireglass batts or roll + reflective foil in the cavity	nil	wall colour: Light (solar absorptance < 0.48)
ceiling and roof - flat ceiling / pitched roof, framed - metal roof, timber - H2 treated softwood	175	ceiling: 4.5 (up), roof: foil backed blanket ceiling; foil backed blanket; roof: foil backed blanket.	nil	roof space ventilation: unventilated; roof colour: medium (solar absorptance 0.6-0.7); ceiling area fully insulated

Note	• Insulation specified in this Certificate must be installed in accordance with the ABCB Housing Provisions (Part 13.2.2) of the National Construction Code.
Note	• If the additional ceiling insulation listed in the table above is greater than R3.0, refer to the ABCB Housing Provisions (Part 13.2.3 (6)) of the National Construction Code.
Note	• In some climate zones, insulation should be installed with due consideration of condensation and associated interaction with adjoining building materials.

Thermal Performance and Materials commitments	Show on DA plans	Show on CC/CDC plans & specs	Certifier check
Ceiling fans			
The applicant must install at least one ceiling fan in at least one daytime habitable space, such as living room.	✔	✔	✔
The applicant must install at least one ceiling fan in each bedroom.	✔	✔	✔

Thermal Performance and Materials commitments	Show on DA plans	Show on CC/CDC plans & specs	Certifier check
Glazed windows, doors and skylights			
The applicant must install the windows, glazed doors and shading devices described in the table below, in accordance with the specifications listed in the table. Relevant overshadowing specifications must be satisfied for each glazed window and door.	✔	✔	✔
The dwelling may have 1 skylight (<0.7 square metres) which is not listed in the table.	✔	✔	✔
The following requirements must also be satisfied in relation to each window and glazed door:	✔	✔	✔
• The applicant must install windows and glazed doors in accordance with the height and width, frame and glazing types listed in the table.	✔	✔	✔
• Each window and glazed door must have a U-value no greater than that listed and a Solar Heat Gain Coefficient (SHGC) within the range listed. Total system U values and SHGC must be calculated in accordance with National Fenestration Rating Council (NFRC) conditions.		✔	✔
The applicant must install the skylights described in the table below, in accordance with the specifications listed in the table. Total skylight area must not exceed 3 square metres (the 3 square metre limit does not include the optional additional skylight of less than 0.7 square metres that does not have to be listed in the table).	✔	✔	✔

Skylight no.	Maximum area (m²)	Skylight specification	Shading device
S01	1.00	aluminium, single clear (U: <=7.3, SHGC: 0.75 - 0.83)	no shading
S02	1.00	aluminium, single clear (U: <=7.3, SHGC: 0.75 - 0.83)	no shading
S03	1.00	aluminium, single clear (U: <=7.3, SHGC: 0.75 - 0.83)	no shading

Glazed window/door no.	Maximum height (mm)	Maximum width (mm)	Frame and glass specification	Shading device (Dimension within 10%)	Overshadowing
North facing					
W02	2100.00	1000.00	thermally broken aluminium, single glazed (U-value: <=3.0, SHGC: >0.49)	none	not overshadowed
W03	850.00	2000.00	thermally broken aluminium, single glazed (U-value: <=3.0, SHGC: >0.49)	none	not overshadowed
W04	850.00	2000.00	thermally broken aluminium, single glazed (U-value: <=3.0, SHGC: >0.49)	none	not overshadowed
W05	850.00	2000.00	thermally broken aluminium, single glazed (U-value: <=3.0, SHGC: >0.49)	none	not overshadowed
W06	650.00	1550.00	thermally broken aluminium, single glazed (U-value: <=3.0, SHGC: >0.49)	none	not overshadowed
East facing					
W01	1200.00	1500.00	thermally broken aluminium, single glazed (U-value: <=3.0, SHGC: >0.49)	none	not overshadowed
West facing					
W07	850.00	2000.00	thermally broken aluminium, single glazed (U-value: <=3.0, SHGC: >0.49)	none	not overshadowed
D01	2400.00	3200.00	thermally broken aluminium, single glazed (U-value: <=3.0, SHGC: >0.49)	none	not overshadowed

ISSUE	DESCRIPTION	DATE	NOTES	SCALE	NORTH	DRAWING TITLE	PROPOSED ATTACHED DUAL OCCUPANCY 26 MARSKELL CIRCUIT MUDGEE					JOB NO. 25008		DATE 4/05/2026	DRAWN P.G	CHECKED P.G	SCALE As Shown on A1	ECOTECH DESIGNS BUILDING DREAMS SUSTAINABLY	
01	ISSUED FOR DA APPROVAL	9/05/2025	The plans, drawings and specifications incorporated in this document shall remain the copyright © of ECOTECH DESIGNS PTY LTD and must not be used, reproduced or copied wholly or in part without prior written consent of ECOTECH DESIGNS PTY LTD. Figured dimensions shall take preference over scaling. Verify all dimensions on site.	1:100 @ A1 or 1:200 @ A3		BASIX COMMITMENTS DRAWING NO CC03													
03	ISSUED FOR DA APPROVAL	8/08/2025																	
04	ISSUED FOR DA APPROVAL	22/10/2025																	
05	ISSUED FOR DA APPROVAL	7/11/2025																	
06	ISSUED FOR CC COORDINATION	2/03/2026																	
07	ISSUED FOR CC APPROVAL	4/05/2026																	

LEGEND - SITE PLAN

- EXTENT OF SITE BOUNDARY
- GRIDLINE
- STORMWATER PIT - REFER TO CIVIL ENGINEERS DETAILS
- DOWNPIPE - REFER TO CIVIL ENGINEERS DETAILS
- EXISTING SITE LEVELS
- PROPOSED TOP OF WALL LEVEL (TOW)
- PROPOSED BOTTOM OF WALL LEVEL (BOM)
- EXTERNAL LANDSCAPE AREA
- CONCRETE TO CIVIL ENGINEERS DETAILS

LEGEND - SUBDIVISION PLAN

- PROPOSED LINE OF SUBDIVISION
- PROPOSED BUILDING FOOTPRINT
- SITE AREA CALCULATION

LEGEND - GFA & CALCULATIONS

- GROSS FLOOR AREA (GFA)
- LANDSCAPING AREA (MIN. 1.5x1.5m)
- PRIVATE OPEN SPACE (MIN. 4x4m)
- ARTICULATION ZONE (1.5m)
- ARTICULATION ELEMENTS (25%)

GENERAL LEGEND

- EXISTING FINISHED FLOOR LEVEL MARKER
- PROPOSED FINISHED FLOOR LEVEL MARKER
- EXISTING FINISHED LEVEL ELEVATION MARKER
- PROPOSED FINISHED LEVEL ELEVATION MARKER
- FLOOR WASTE PENETRATION
- SMOKE ALARM TO AS3786
- DIRECTION AND ANGLE OF INCLINING GRADIENT
- REVIEW / REVISION CLOUD
- PENETRATION ABOVE
- FLOOR PENETRATION BELOW

HYDRAULIC / STORMWATER LEGEND

- DOWNPIPE - REFER TO CIVIL ENGINEERS DETAILS
- PLANTER DRAIN OUTLET
- SPOOD DRAIN OUTLET
- RAIN WATER OUTLET
- STORMWATER PIT - REFER TO CIVIL ENGINEERS DETAILS
- RAIN WATER TANK TO BASIX REQUIREMENTS AND STORMWATER ENGINEERS DETAILS

LEGEND - CONCRETE SETOUT

- INTERNAL FINISHED SLAB LEVEL
- 50MM SETDOWN TO WET AREA
- 100MM SETDOWN TO EXTERNAL

LEGEND - REFLECTED CEILING PLAN

- MOISTURE RESISTANT BOARD - PAINT FINISH
- PLASTER BOARD CEILING - PAINT FINISH
- PLASTER BOARD CEILING - PAINT FINISH
- CEILING/ SOFFIT HEIGHT FROM FFL
- RECESS FOR CURTAIN/BLIND

LEGEND - DEMOLITION PLAN

- EXISTING STRUCTURES TO BE DEMOLISHED. REPAIR & REINSTATE ADJOINING SURFACES.
- EXISTING SITE TO BE REMOVED / DEMOLISHED
- EXISTING TREES TO REMAIN. REFER ALSO TO LANDSCAPE DRAWING.
- EXISTING TREES TO BE REMOVED. REFER ALSO TO LANDSCAPE DRAWING.

-PERFORM ALL THE DEMOLITION AS SHOWN ON THE DRAWING AND/OR AS NECESSARY REQUIRED CARRYING OUT THE WORKS UNDER THE CONTRACT.

-NB: CARE MUST BE TAKEN WHILE CARRING OUT THE WORKS.

-PROTECT EXISTING PROPERTY FROM DAMAGE BY APPROPRIATE MEANS INCLUDING SHORING, STRUTTING, PROTECTIVE SCREENS, SHEETING AND THE LIKE.

-REPAIR & REINSTATE ANY SUCH DAMAGE TO MATCH EXISTING.

-EXISTING SERVICES: DEAL AS APPROPRIATE WITH EXISTING SERVICES INCLUDED IN OR ENCOUNTERED DURING THE COURSE OF THE DEMOLITIONS.


-BEFORE DEMOLISHING AND REMOVING PARTS OF BUILDING HAVING ELECTRICAL WIRING, GAS, SEWER AND WATER PIPES, CONDUIT OR SIMILAR ITEMS EMBEDDED IN THEM, NOTIFY THE PROJECT MANAGER/ SUPERINTENDENT, AUTHORITIES HAVING JURISDICTION, AND MAKE SURE THAT THESE ITEMS ARE OUT OF SERVICE SO THAT THEY CAN BE REMOVED WITHOUT DANGER.

NOTES

- COMMON WALL FIRE SEPARATION CLAUSE 9.3.1 OF THE HOUSING PROVISIONS 2022 (FRL 60/60/60)
- COMMON WALL SOUND SEPARATION CLAUSE 10.7.1 OF THE HOUSING PROVISIONS 2022
- MECHANICAL VENTILATION CLAUSE 10.6.2 OF THE HOUSING PROVISIONS 2022
- SMOKE ALARMS CLAUSE 9.5.4 OF THE HOUSING PROVISIONS 2022
- BALUSTRADES INSTALLATION CLAUSE 11.3.4 OF THE HOUSING PROVISIONS 2022
- PROTECTION OF OPERABLE WINDOWS CLAUSE 11.3.7 OF THE HOUSING PROVISIONS 2022

LEGEND - WALL TYPES

- 250mm BRICK VENEER WALL
- 110mm FACE BRICK + 50mm CAVITY + 90mm TIMBER STUD + 10mm GYPROCK
- 230mm BRICK VENEER WALL
- 110mm FACE BRICK + 10mm CAVITY + 110mm FACE BRICK
- 90mm STUD WALL
- 10mm GYPROCK + 90mm TIMBER STUD + 10mm GYPROCK
- CSR 360 TIMBER FRAMED PARTY WALL SYSTEM
- 10mm GYPROCK + 90mm TIMBER STUD + 20mm CAVITY + 25mm GYPROCK SHAFT LINER PANEL + 90mm TIMBER STUD + 10mm GYPROCK
- 225mm HERAL VENEER WALL
- 10mm ACRYLIC RENDER + 100mm NRG
- Greenboard + 25mm CAVITY + 90mm TIMBER STUD + 10mm GYPROCK

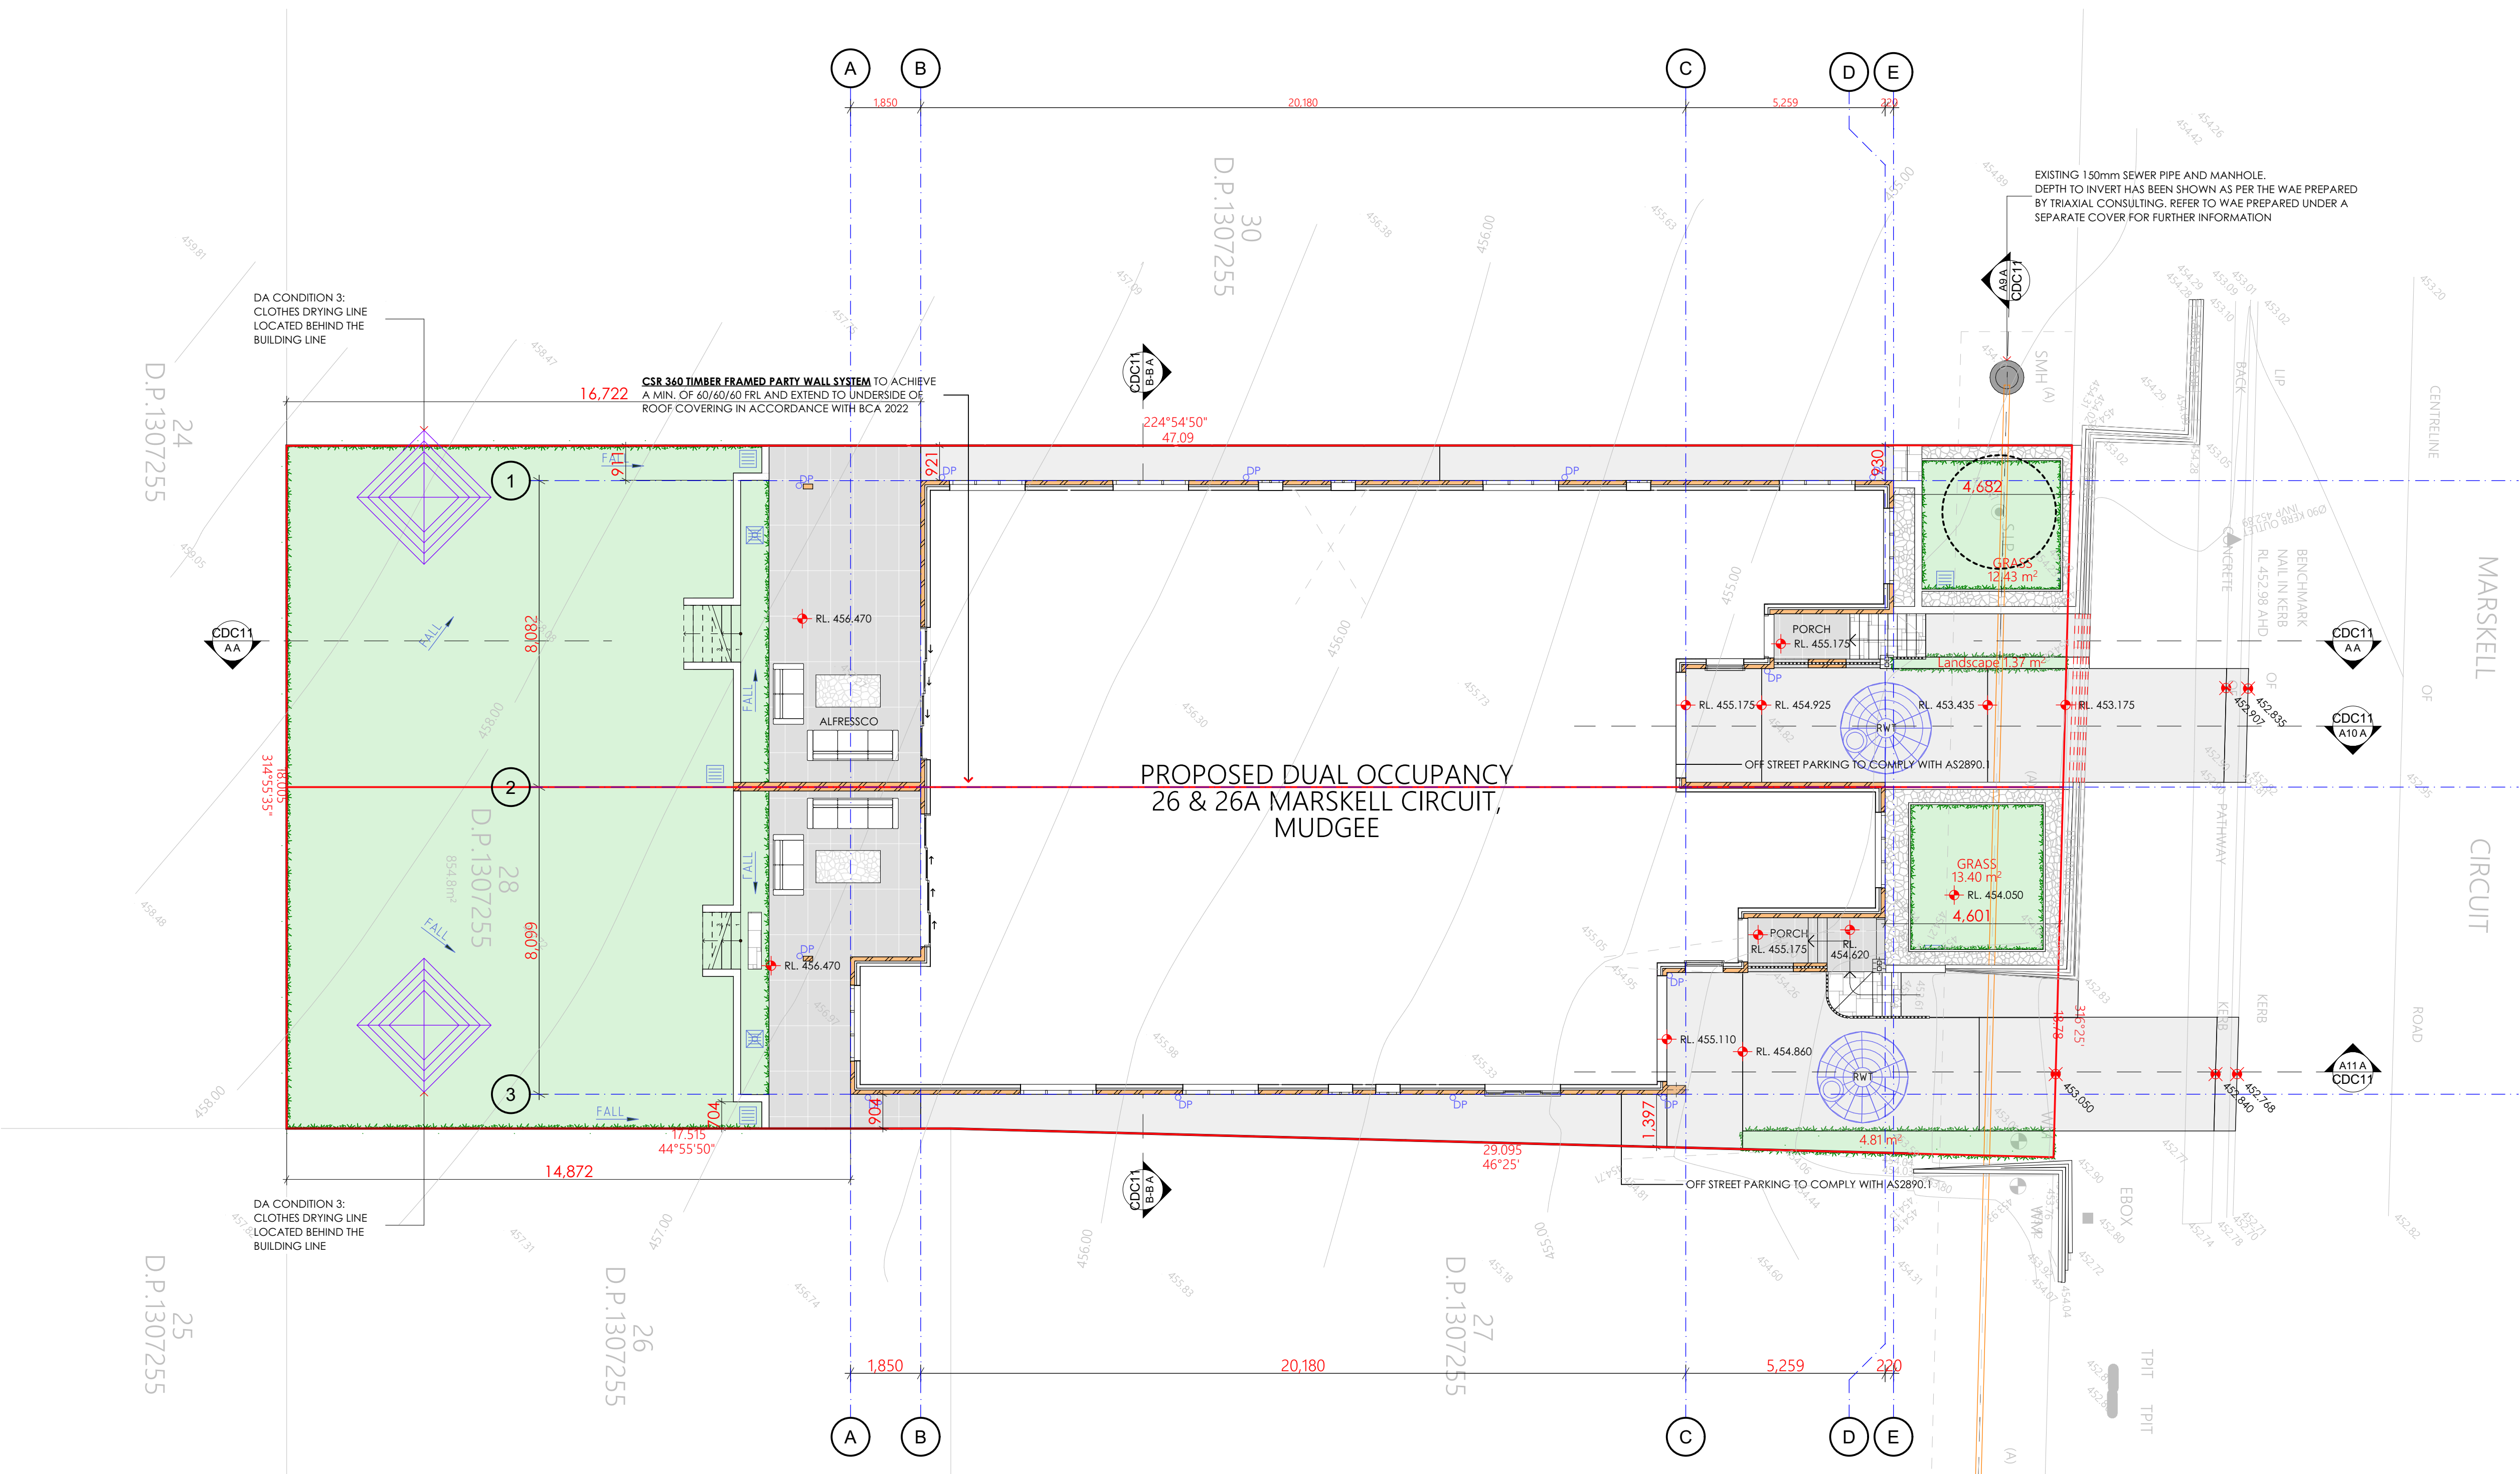


SITE PLAN
1:100

ISSUE	DESCRIPTION	DATE
01	ISSUED FOR DA APPROVAL	9/05/2025
03	ISSUED FOR DA APPROVAL	8/08/2025
04	ISSUED FOR DA APPROVAL	22/10/2025
05	ISSUED FOR DA APPROVAL	7/11/2025
06	ISSUED FOR CC COORDINATION	2/03/2026
07	ISSUED FOR CC APPROVAL	4/05/2026

NOTES
The plans, drawings and specifications incorporated in this document shall remain the copyright © of ECOTECH DESIGNS PTY LTD and must not be used, reproduced or copied wholly or in part without prior written consent of ECOTECH DESIGNS PTY LTD.
Figured dimensions shall take preference over scaling. Verify all dimensions on site.

SCALE
1:100 @ A1 or 1:200 @ A3

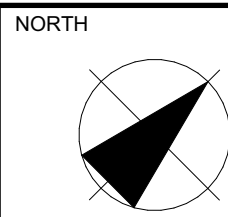

DRAWING TITLE
SITE PLAN
DRAWING NO
CC04

PROPOSED ATTACHED DUAL OCCUPANCY
26 MARSKELL CIRCUIT MUDGEE

JOB NO. 25008	DATE 4/05/2026	DRAWN P.G	CHECKED P.G	SCALE As Shown on A1
------------------	-------------------	--------------	----------------	-------------------------



- EXTENT OF SITE BOUNDARY
- GRIDLINE
- STORMWATER PIT - REFER TO CIVIL ENGINEERS DETAILS
- DOWNPIPE - REFER TO CIVIL ENGINEERS DETAILS
- EXISTING SITE LEVELS
- PROPOSED TOP OF WALL LEVEL (TOW)
- PROPOSED BOTTOM OF WALL LEVEL (BOM)
- EXTERNAL LANDSCAPE AREA
- CONCRETE TO CIVIL ENGINEERS DETAILS

 PROPOSED LINE OF SUBDIVISION
 PROPOSED BUILDING FOOTPRINT
 SITE AREA CALCULATION

	GROSS FLOOR AREA (GFA)
	LANDSCAPING AREA (MIN. 1.5x1.5m)
	PRIVATE OPEN SPACE (MIN. 4x4m)
	ARTICULATION ZONE (1.5m)
	ARTICULATION ELEMENTS (25%)

	EX RL.0.000	EXISTING FINISHED FLOOR LEVEL MARKER
	RL.0.000	PROPOSED FINISHED FLOOR LEVEL MARKER
	EX RL.0.000	EXISTING FINISHED FLOOR ELEVATION MARKER
	RL.0.000	PROPOSED FINISHED FLOOR ELEVATION MARKER
	F.W	FLOOR WASTE PENETRATION
	S.A	SMOKE ALARM TO AS3786
	FALL 1:8.5	DIRECTION AND ANGLE OF INCLINING GRADIENT
		REVIEW / REVISION CLOUD
		PENETRATION ABOVE
		FLOOR PENETRATION BELOW

ODP	DOWNPIPE - REFER TO CIVIL ENGINEERS DETAILS
OPDO	PLANTER DRAIN OUTLET
OSDO	SPOOD DRAIN OUTLET
ORWO	RAIN WATER OUTLET
	STORMWATER PIT - REFER TO CIVIL ENGINEERS DETAILS
	RAIN WATER TANK TO BASIX REQUIREMENTS AND STORMWATER ENGINEERS DETAILS

 INTERNAL FINISHED SLAB LEVEL
 50MM SETDOWN TO WET AREA
 100MM SETDOWN TO EXTERNAL

	MOISTURE RESISTANT BOARD - PAINT FINISH
	PLASTER BOARD CEILING - PAINT FINISH
	PLASTER BOARD CEILING - PAINT FINISH
	CEILING/ SOFFIT HEIGHT FROM FFL
	RECESS FOR CURTAIN/BLIND

 EXISTING STRUCTURES TO BE DEMOLISHED.
REPAIR & REINSTATE ADJOINING SURFACES.

 EXISTING SITE TO BE REMOVED / DEMOLISHED
EXISTING TREES TO REMAIN. REFER ALSO TO
LANDSCAPE DRAWING.

 EXISTING TREES TO BE REMOVED. REFER ALSO
TO LANDSCAPE DRAWING.

-PERFORM ALL THE DEMOLITION AS SHOWN ON THE DRAWING AND/OR AS NECESSARY REQUIRED CARRYING OUT THE WORKS UNDER THE CONTRACT.

-NB: CARE MUST BE TAKEN WHILE CARRING OUT THE WORKS.

-PROTECT EXISTING PROPERTY FROM DAMAGE BY APPROPRIATE MEANS INCLUDING SHORING, STRUTTING, PROTECTIVE SCREENS, SHEETING AND THE LIKE.


-REPAIR & REINSTATE ANY SUCH DAMAGE TO MATCH EXISTING.

-EXISTING SERVICES: DEAL AS APPROPRIATE WITH EXISTING SERVICES INCLUDED IN OR ENCOUNTERED DURING THE COURSE OF THE DEMOLITIONS.

-BEFORE DEMOLISHING AND REMOVING PARTS OF BUILDING HAVING ELECTRICAL WIRING, GAS, SEWER AND WATER PIPES, CONDUIT OR SIMILAR ITEMS EMBEDDED IN THEM, NOTIFY THE PROJECT MANAGER/ SUPERINTENDENT, AUTHORITIES HAVING JURISDICTION, AND MAKE SURE THAT THESE ITEMS ARE OUT OF SERVICE SO THAT THEY CAN BE REMOVED WITHOUT DANGER.

- COMMON WALL FIRE SEPARATION CLAUSE 9.3.1 OF THE HOUSING PROVISIONS 2022 [FRL 60/60/60]
- COMMON WALL SOUND SEPARATION CLAUSE 10.7.1 OF THE HOUSING PROVISIONS 2022
- MECHANICAL VENTILATION CLAUSE 10.6.2 OF THE HOUSING PROVISIONS 2022
- SMOKE ALARMS CLAUSE 9.5.4 OF THE HOUSING PROVISIONS 2022
- BALUSTRADES INSTALLATION CLAUSE 11.3.4 OF THE HOUSING PROVISIONS 2022
- PROTECTION OF OPERABLE WINDOWS CLAUSE 11.3.7 OF THE HOUSING PROVISIONS 2022

	250mm BRICK VENEER WALL 110mm FACE BRICK + 50mm CAVITY + 90mm TIMBER STUD + 10mm GYPROCK
	230mm BRICK VENEER WALL 110mm FACE BRICK + 10mm CAVITY + 110mm FACE BRICK
	90mm STUD WALL 10mm GYPROCK + 90mm TIMBER STUD + 10mm GYPROCK
	CSB 350 TIMBER FRAMED PARTY WALL SYSTEM 10mm GYPROCK + 90mm TIMBER STUD + 20mm CAVITY + 25mm GYPROCK SHAFT LINER PANEL + 90mm TIMBER STUD + 10mm GYPROCK
	225mm HEBEL VENEER WALL 10mm ACRYLIC RENDER + 100mm NRG Greenboard + 25mm CAVITY + 90mm TIMBER STUD + 10mm GYPROCK

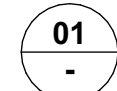

PLAN OF TORRENS TITLE SUBDIVISION

1:100


ISSUE	DESCRIPTION	DATE
01	ISSUED FOR DA APPROVAL	9/05/2025
03	ISSUED FOR DA APPROVAL	8/08/2025
04	ISSUED FOR DA APPROVAL	22/10/2025
05	ISSUED FOR DA APPROVAL	7/11/2025
06	ISSUED FOR CC COORDINATRION	2/03/2026
07	ISSUED FOR CC APPROVAL	4/05/2026

NOTES

The plans, drawings and specifications incorporated in this document shall remain the copyright © of ECOTECH DESIGNS PTY LTD and must not be used, reproduced or copied wholly or in part without prior written consent of ECOTECH DESIGNS PTY LTD.

Figured dimensions shall take preference over scaling. Verify all dimensions on site.

1:100 @ A1 or 1:200 @ A3








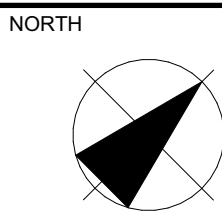


DRAWING TITLE
**PLAN OF TORRENS TITLE
SUBDIVISION**

DRAWING NO
CC05

PROPOSED ATTACHED DUAL OCCUPANCY 26 MARSELLI CIRCUIT MUDGEJE				
JOB NO. 25008	DATE 4/05/2026	DRAWN P.G	CHECKED P.G	SCALE As Shown on A1



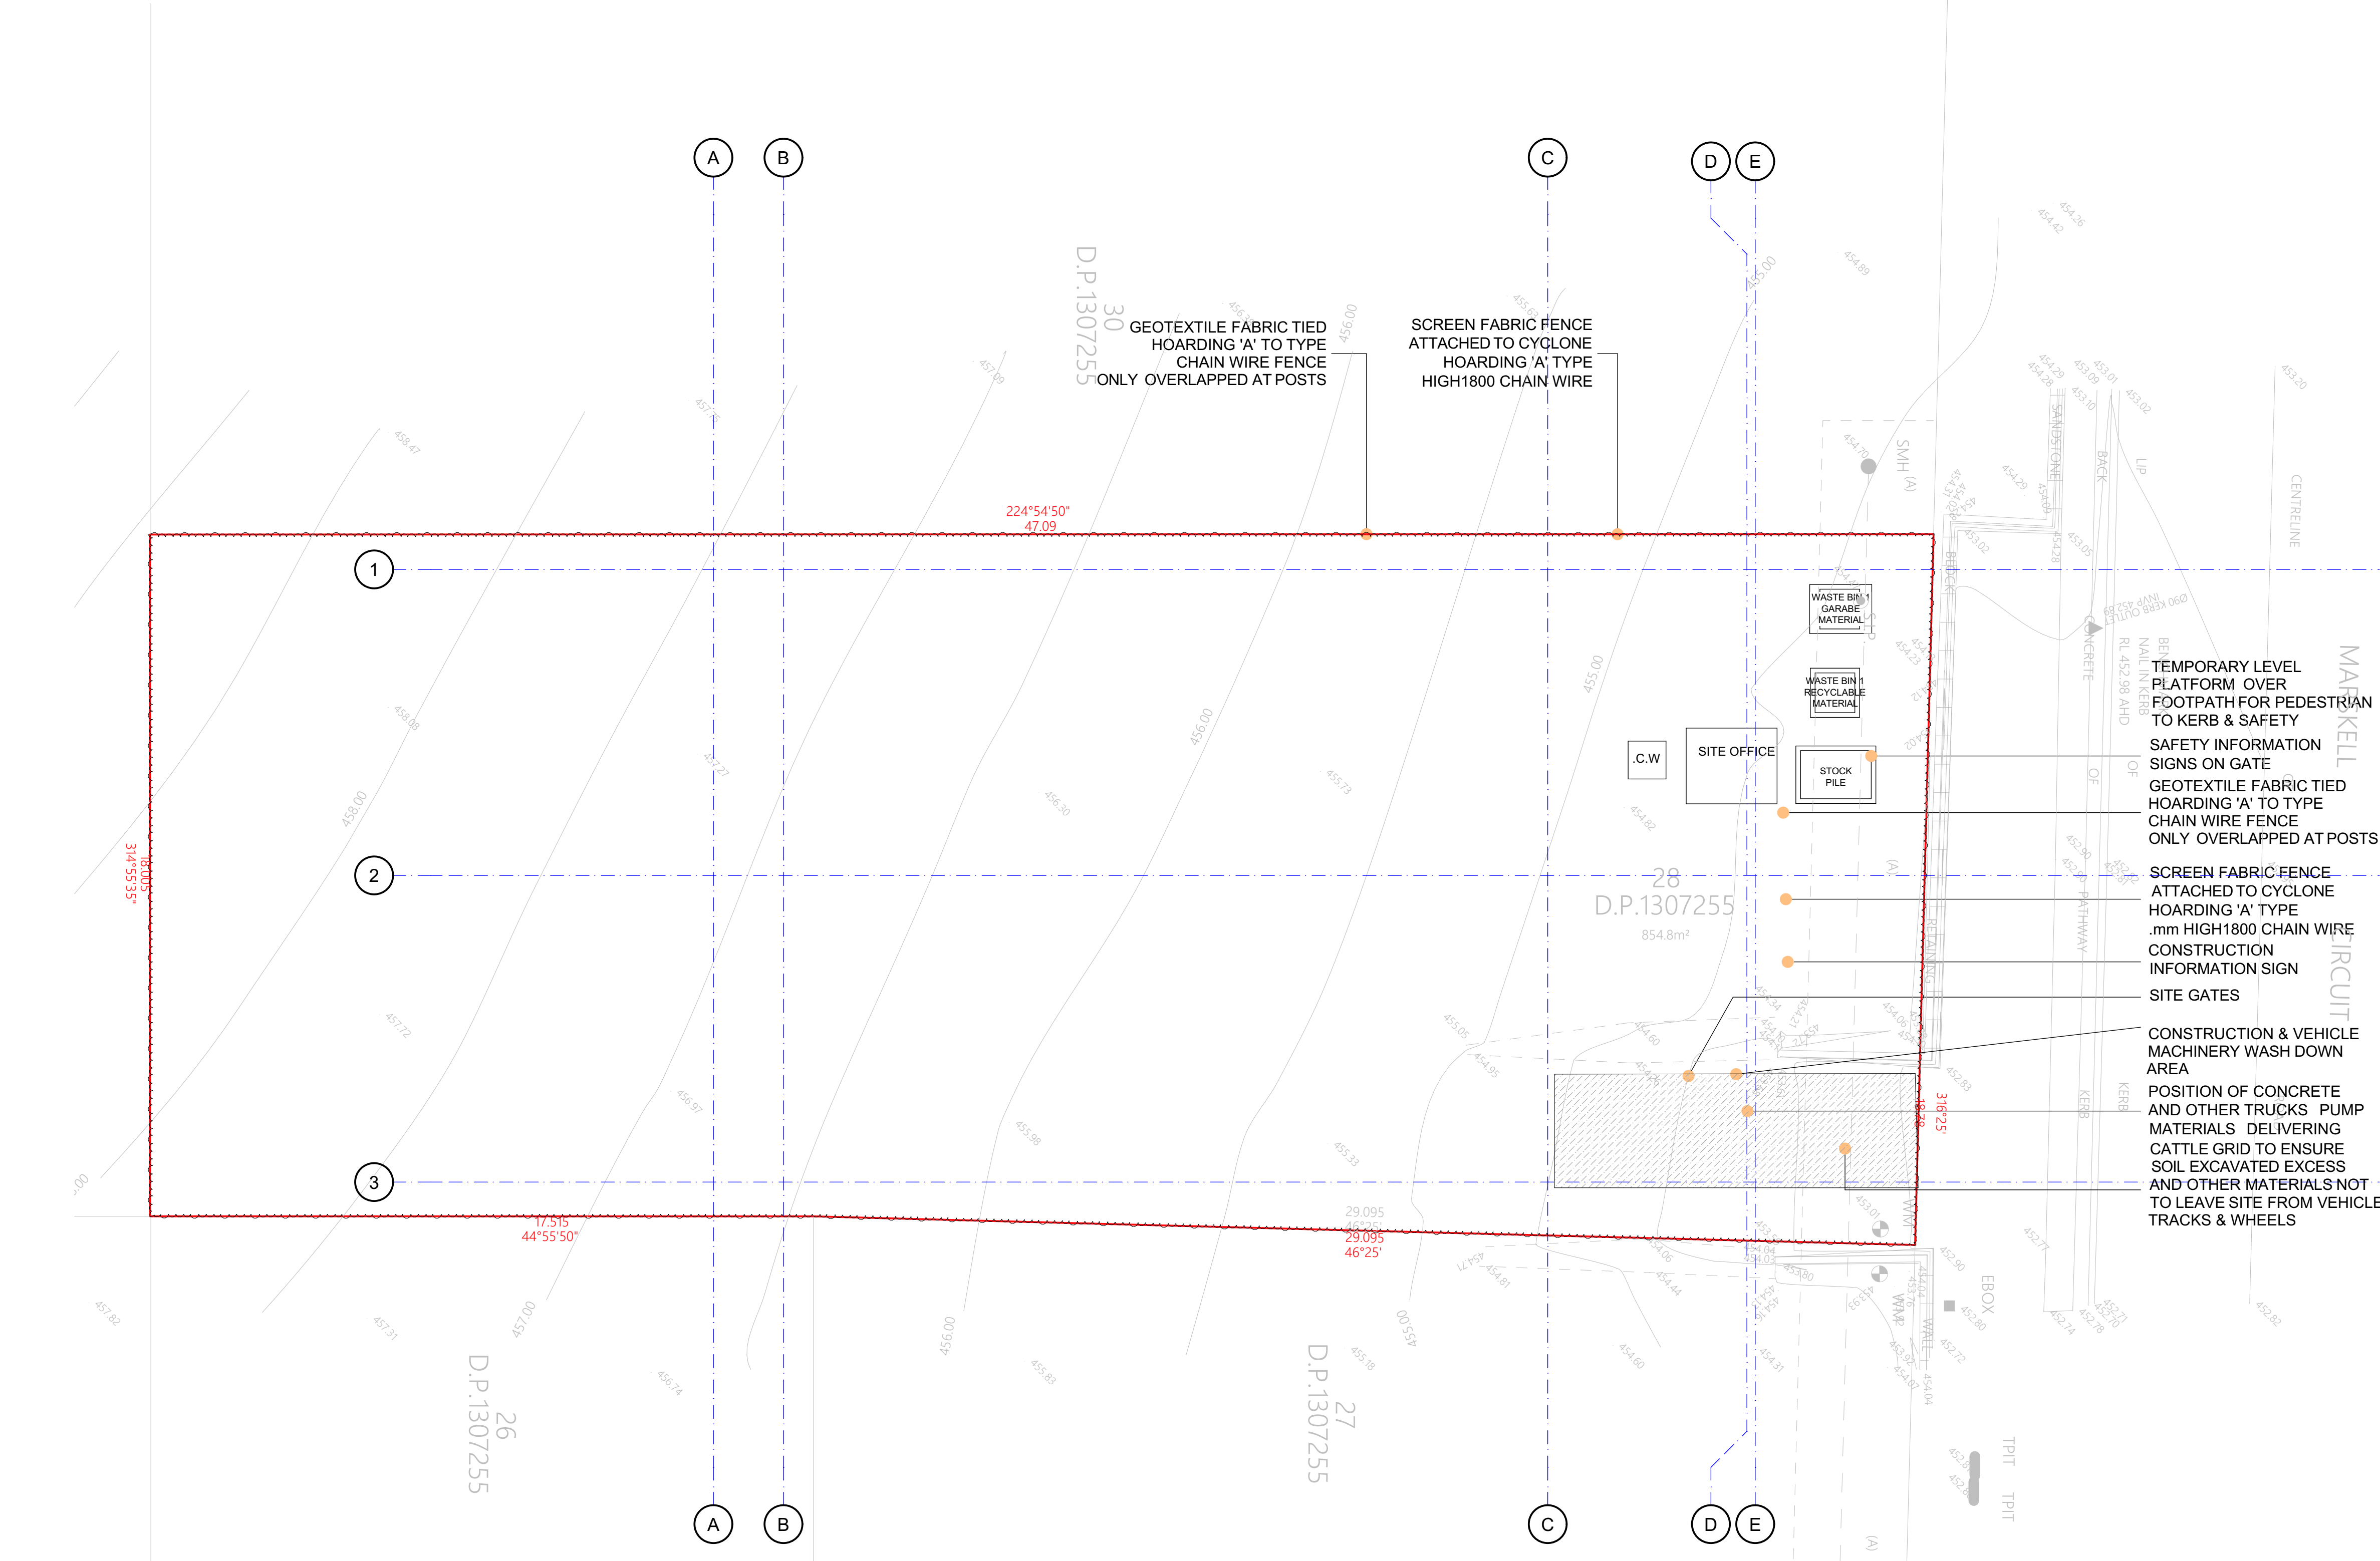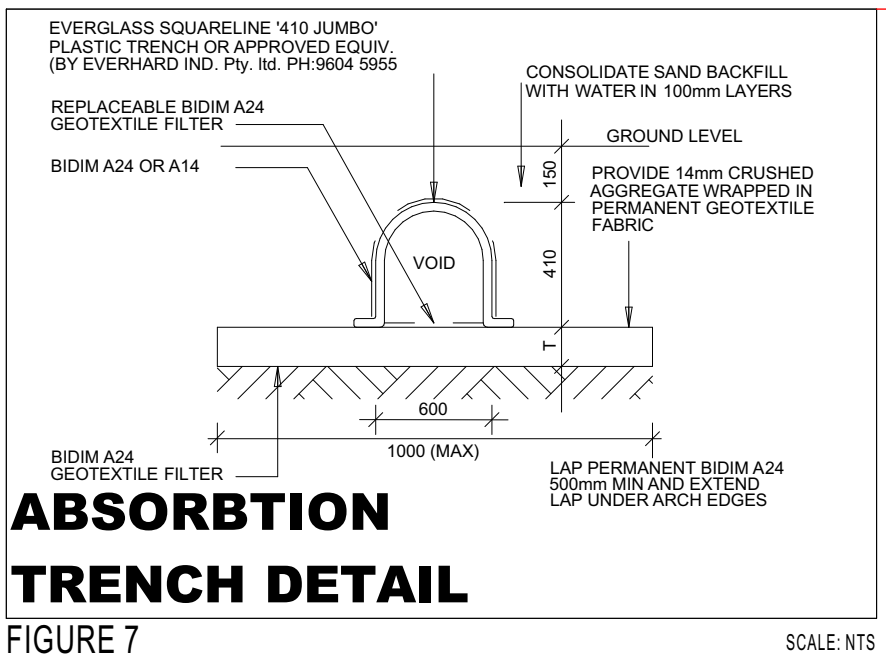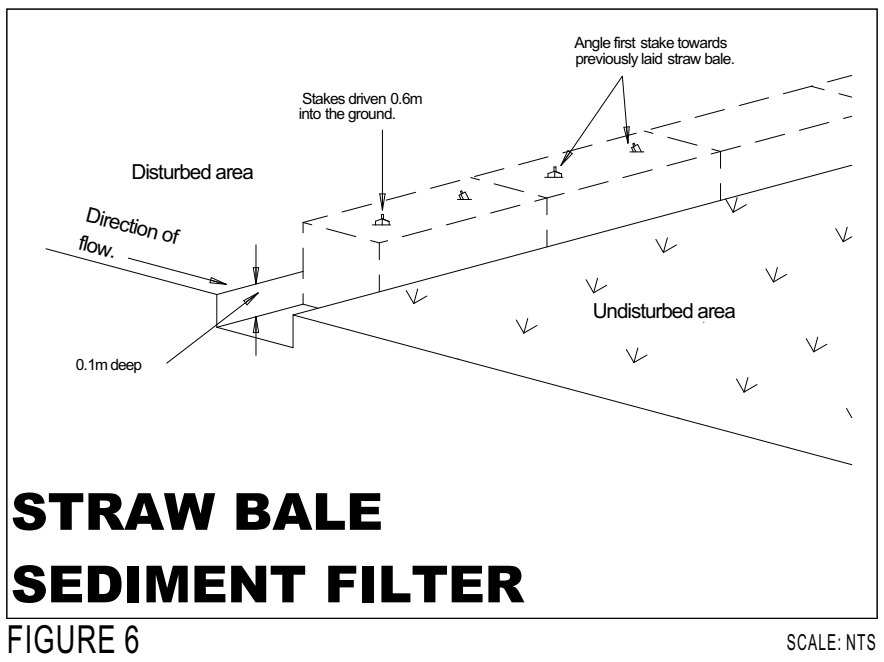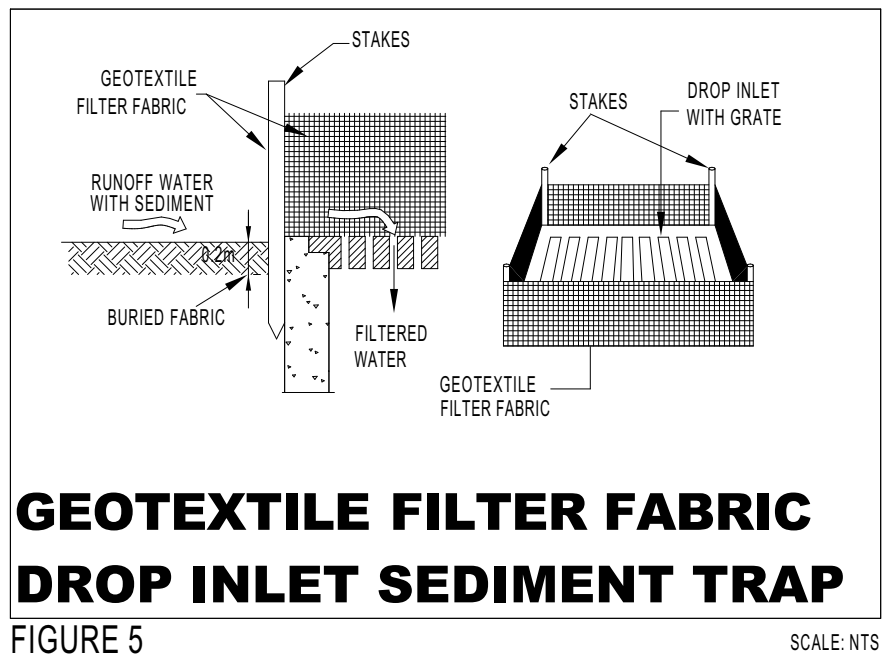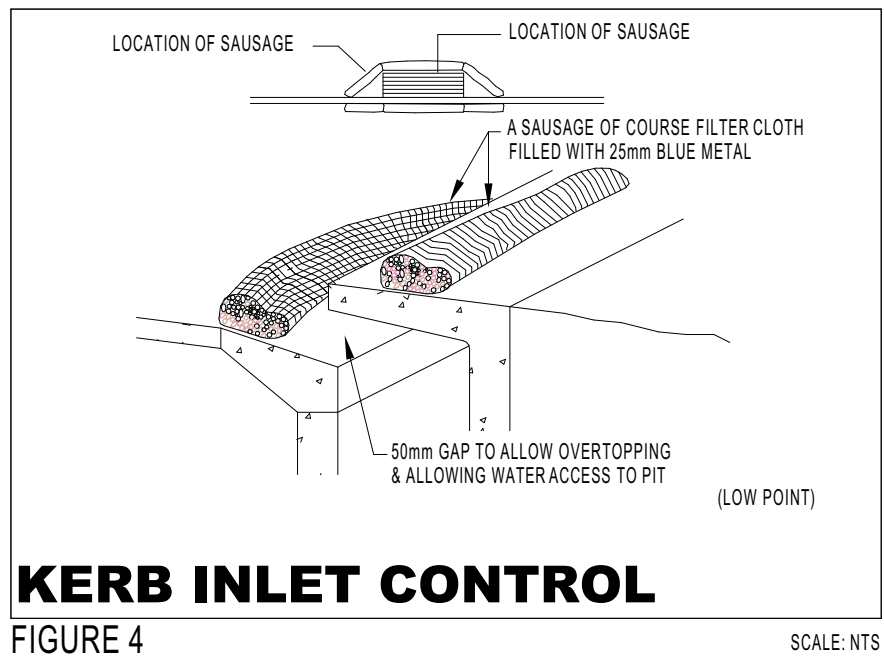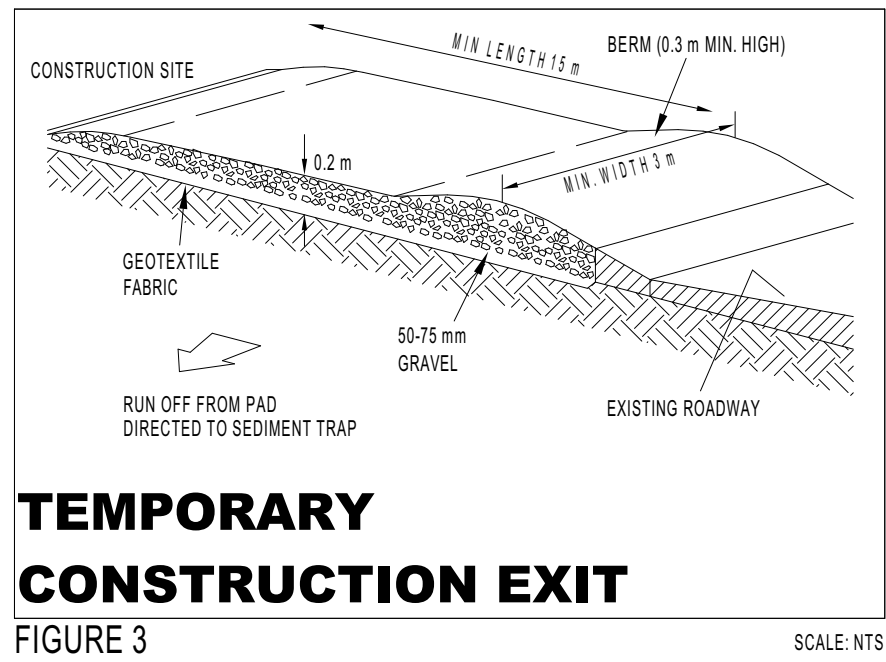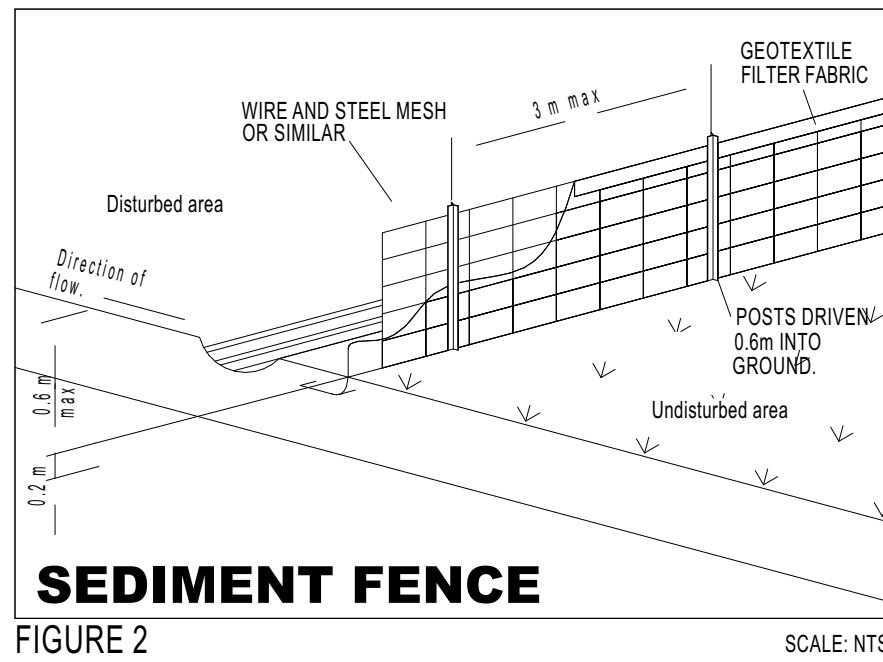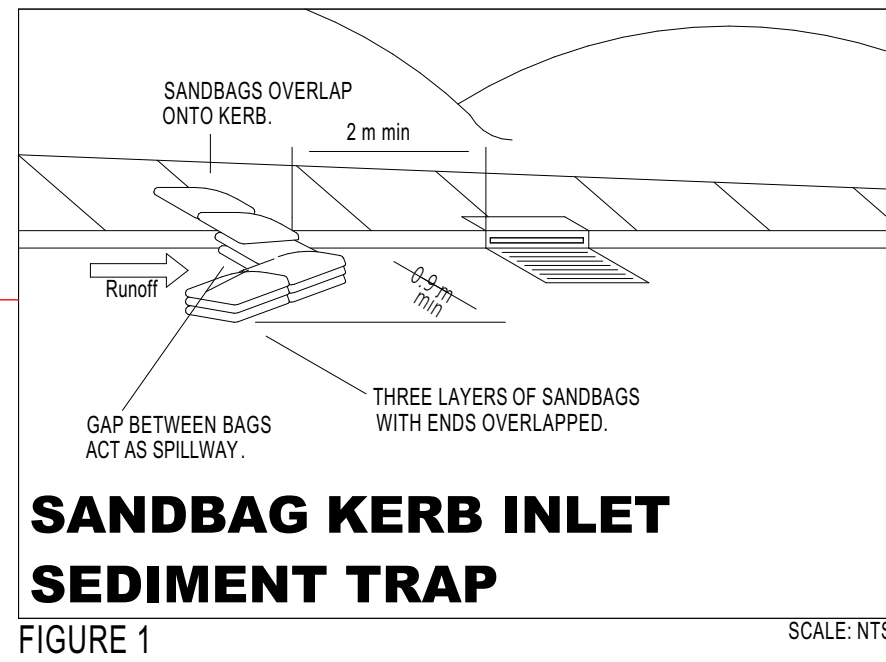

EROSION AND SEDIMENTATION CONTROL NOTES:	
1. BUILDER SHALL PROVIDE SEDIMENT FENCING MATERIAL DURING CONSTRUCTION TO THE LOW SIDE BOUNDARIES. THE SEDIMENT FENCING MATERIAL TO CYCLONE WIRE SECURITY FENCE. SEDIMENT CONTROL FABRIC SHALL BE AN APPROVED MATERIAL (Eg. HUMES PROPEX SILT STOP) STANDING 300mm. ABOVE GROUND AND EXTENDING 200 BELOW GROUND AND TO EXTENT NOTED.	
2. EXISTING AND NEW DRAINS LOCATED WITHIN THE SITE SHALL ALSO BE ISOLATED BY SEDIMENT FENCING MATERIAL UNTIL PAVEMENTS COMPLETED.	
3. NO PARKING OR STOCK PILING OF MATERIALS IS PERMITTED ON THE LOWER SIDE OF THE SEDIMENT FENCE.	
4. GRASS VERGES SHALL BE MAINTAINED AS MUCH AS PRACTICAL TO PROVIDE A BUFFER ZONE TO THE CONSTRUCTION SITE.	
5. ROOF DRAINAGE IS TO BE CONNECTED TO THE STORMWATER SYSTEM AS SOON AS PRACTICAL.	
6. CONSTRUCTION ENTRY / EXIT SHALL BE AS PER DETAIL. BUILDER SHALL ENSURE ALL DROPPABLE SOIL AND SEDIMENT IS REMOVED PRIOR TO CONSTRUCTION TRAFFIC EXITING SITE. BUILDER SHALL ENSURE ALL CONSTRUCTION TRAFFIC ENTERING AND LEAVING THE SITE, DO SO, IN A FORWARD DIRECTION.	
DEMOLITION NOTES:	
HATCHED & DASHED AREAS INDICATES ITEMS & STRUCTURES TO BE DEMOLISHED	
EXISTING SERVICES: ELECTRICITY TO BE DISCONNECTED AND RECONNECTED THROUGH TEMPORARY SUPPLY (MAINTAIN METER).	
SEWERAGE AND STORMWATER TO BE CAPPED OFF WHERE REQUIRED. WATER SUPPLY TO BE CAPPED OFF WHERE NECESSARY TO ALLOW FOR CONSTRUCTION. TELEPHONE LINE TO BE RELOCATED IF NECESSARY TO TELSTRAS REQUIREMENTS	
MAINTAIN AND PROTECT CONSTRUCTION AND PROPERTY ON ADJOINING BLOCKS FROM DEMOLITION ACTIVITIES DISPOSE OF ALL DEMOLITION MATERIALS AND RUBBISH IN A MANNER ACCEPTABLE TO COUNCIL.	
PROPOSED METHOD: DISMANTLE ROOF, TRIMMER TRUSSES AND TIMBER BEAMS FOR SALVAGE AND RE-USE. REMOVAL OF ALL GLASS AND WINDOWS FOR RE-USE. BRICK WALLS TO BE DISMANTLED BY HAND AND SOLD. ANY BROKEN REMAINS TO BE CRUSHED FOR RECYCLING. INTERNAL GYPROCK WALLS AND FRAMES TO BE DISMANTLED BY HAND AND TAKEN TO TIP. THE REMAINS WOULD THEN BE MADE UP OF CONCRETE SLABS, VERANDASHS, CONCRETE DRIVEWAYS AND CARPARKING. THIS WOULD BE DELIVERED TO RECYCLERS.	
POLLUTION CONTROL MEASURES SHALL BE IMPLEMENTED IN ACCORDANCE WITH AUSTRALIAN STANDARDS AND THE REQUIREMENTS OF ENVIRONMENT ACT.	
ASBESTOS FIBRO SHEET WHERE ENCOUNTERED WILL BE DISPOSED OF BY A LICENCED ASBESTOS REMOVING CONTRACTOR ACCORDING WASTE SERVICES NSW ASBESTOS REMOVAL STANDARDS.	
VEGETATION - TREES TO BE REMOVED ARE TO BE DISPOSED IN ACCORDANCE WITH REQUIREMENTS OF ENVIRONMENT ACT.	
CONSTRUCTION MANAGEMENT NOTES:	
1. SITE SIGANCE SHALL BE ERECTED ON SITE IN A PROMINENT POSITION STATING THE FOLLOWING: - THE NAME, ADDRESS AND TELEPHONE NUMBERS OF THE PCA - THE NAME OF THE PERSON IN CHARGE OF THE WORK SITE & A - TELEPHONE NUMBER IN WHICH THAT PERSON MAY BE CONTACTED. - THAT UNAUTHORISED ENTRY TO THE WORK SITE IS PROHIBITED.	
2. ALL MATERIALS MUST BE STORED WHOLLY WITHIN THE PROPERTY BOUNDARIES AND MUST NOT BE PLACED ON THE FOOTPATH OR ROADWAY.	
3. ALL BUILDING WORKS IS RESTRICTED TO THE HOURS OF: 7:00 AM - 5:00 PM MONDAY TO SATURDAY. EXPECT THAT ON SATURDAY NO MECHANICAL BUILDING EQUIPMENT CAN BE USED AFTER 12:00 NOON. NO WORK PERMITTED ON SUNDAYS OR PUBLIC HOLIDAYS.	
4. ALL BUILDING CONSTRUCTION WORK MUST COMPLY WITH THE NATIONAL CONSTRUCTION CODE.	
5. DISPLAY COUNCIL'S WARNING SIGN FOR SOIL & WATER MANAGEMENT ON THE MOST PROMINENT POINT ON THE BUIDING SITE, VISIBLE TO BOTH THE STREET AND WORKERS.	
6. KEEP DRAINS, GUTTERS, ROADWAYS AND ACCESSWAYS FREE OF SOIL, CLAY AND SEDIMENT. WHERE REQUIRED, GUTTERS AND ROADWAYS MUST BE SWEEP REGULARLY TO MAINTAIN THEM FREE FROM SEDIMENT. DO NOT HOSE DOWN.	
7. PROVIDE A VEHICLE WASHDOWN AREA AT THE EXIT POINT OF THE SITE TO REMOVE LOOSE MATERIAL FROM ALL VEHICLES AND MACHINERY BEFORE ENTERING THE ROAD RESERVE. ALL RUN-OFF MUST DRAIN TO AN APPROVED SILT TRAP PRIOR TO DISPOSAL TO THE STORMWATER DRAINAGE SYSTEM IN ACCORDANCE WITH COUNCIL'S S.M.M.	
8. METHOD OF SUPPORT TO EXCAVATION ADJACENT TO ADJOINING PROPERTIES OR ROAD RESERVE TO BE PROPOSED BY STRUCTURAL / CIVIL ENGINEER.	
9. ALL CONSTRUCTION VEHICLES REQUIRED TO ENTER & EXIT THE SITE MUST DO SO IN A FORWARD DIRECTION IN ORDER TO ENSURE SAFE INGRESS AND EGRESS FROM THE SITE.	
10. WHERE PRACTICLE THE LOADING AND UNLOADING OF EXCAVATION AND CONSTRUCTION MACHINERY AND BUILDING MATERIALS IS TO BE CONDUCTED WITHIN THE PROPERTY BOUNDARY.	
11. SITE ENTRANCES AND EXITS MUST BE CONTROLLED BY A CERTIFIED TRAFFIC CONTROLLER TO SAFETY MANAGE PEDESTRIANS AND CONSTRUCTION RELATED VEHICLES IN THE FRONTAGE ROADWAY.	
STOCKPILE COVERED WITH GEOTEXTILE FABRIC AND WEIGHED DOWN WITH BRICKS OR ROCKS AND SAND AND MATERIAL DROP OFF AREA	
NOTE: EXISTING DRIVEWAY TO BE USED DURING CONSTRUCTION.	

LEGEND - DEMOLITION PLAN

--- EXTENT OF SITE BOUNDARY

EXISTING TREES TO REMAIN. REFER ALSO TO LANDSCAPE DRAWING.


+ EXISTING LEVELS



ISSUE	DESCRIPTION	DATE
01	ISSUED FOR DA APPROVAL	9/05/2025
03	ISSUED FOR DA APPROVAL	8/08/2025
04	ISSUED FOR DA APPROVAL	22/10/2025
05	ISSUED FOR DA APPROVAL	7/11/2025
06	ISSUED FOR CC COORDINATRION	2/03/2026
07	ISSUED FOR CC APPROVAL	4/05/2026

NOTES
The plans, drawings and specifications incorporated in this document shall remain the copyright © of ECOTECH DESIGNS PTY LTD and must not be used, reproduced or copied wholly or in part without prior written consent of ECOTECH DESIGNS PTY LTD.
Figured dimensions shall take preference over scaling. Verify all dimensions on site.

SCALE
1:100 @ A1 or 1:200 @ A3

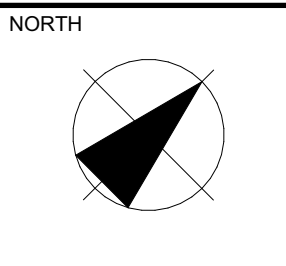

DRAWING TITLE
SEDIMENT AND EROSION CONTROL PLAN
DRAWING NO
CC06

DRAWING TITLE
SEDIMENT AND EROSION CONTROL PLAN
DRAWING NO
CC06

PROPOSED ATTACHED DUAL OCCUPANCY				
26 MARSKELL CIRCUIT MUDGEE				
JOB NO.	DATE	DRAWN	CHECKED	SCALE
25008	4/05/2026	P.G	P.G	As Shown on A1

ECOTECH DESIGNS	
BUILDING DREAMS SUSTAINABLY	

LEGEND - SITE PLAN

- EXTENT OF SITE BOUNDARY
- GRIDLINE
- STORMWATER PIT - REFER TO CIVIL ENGINEERS DETAILS
- DOWNPIPE - REFER TO CIVIL ENGINEERS DETAILS
- EXISTING SITE LEVELS
- PROPOSED TOP OF WALL LEVEL (TOW)
- PROPOSED BOTTOM OF WALL LEVEL (BOM)
- EXTERNAL LANDSCAPE AREA
- CONCRETE TO CIVIL ENGINEERS DETAILS

LEGEND - SUBDIVISION PLAN

- PROPOSED LINE OF SUBDIVISION
- PROPOSED BUILDING FOOTPRINT
- SITE AREA CALCULATION

LEGEND - GFA & CALCULATIONS

- GROSS FLOOR AREA (GFA)
- LANDSCAPING AREA (MIN. 1.5x1.5m)
- PRIVATE OPEN SPACE (MIN. 4x4m)
- ARTICULATION ZONE (1.5m)
- ARTICULATION ELEMENTS (25%)

GENERAL LEGEND

- EXISTING FINISHED FLOOR LEVEL MARKER
- PROPOSED FINISHED FLOOR LEVEL MARKER
- EXISTING FINISHED LEVEL ELEVATION MARKER
- PROPOSED FINISHED LEVEL ELEVATION MARKER
- FLOOR WASTE PENETRATION
- SMOKE ALARM TO AS3786
- DIRECTION AND ANGLE OF INCLINING GRADIENT
- REVIEW / REVISION CLOUD
- PENETRATION ABOVE
- FLOOR PENETRATION BELOW

HYDRAULIC / STORMWATER LEGEND

- DOWNPIPE - REFER TO CIVIL ENGINEERS DETAILS
- PLANTER DRAIN OUTLET
- SPOOD DRAIN OUTLET
- RAIN WATER OUTLET
- STORMWATER PIT - REFER TO CIVIL ENGINEERS DETAILS
- RAIN WATER TANK TO BASIX REQUIREMENTS AND STORMWATER ENGINEERS DETAILS

LEGEND - CONCRETE SETOUT

- INTERNAL FINISHED SLAB LEVEL
- 50MM SETDOWN TO WET AREA
- 100MM SETDOWN TO EXTERNAL

LEGEND - REFLECTED CEILING PLAN

- MOISTURE RESISTANT BOARD - PAINT FINISH
- PLASTER BOARD CEILING - PAINT FINISH
- PLASTER BOARD CEILING - PAINT FINISH
- CEILING/ SOFFIT HEIGHT FROM FFL
- RECESS FOR CURTAIN/BLIND

LEGEND - DEMOLITION PLAN

- EXISTING STRUCTURES TO BE DEMOLISHED. REPAIR & REINSTATE ADJOINING SURFACES.
- EXISTING SITE TO BE REMOVED / DEMOLISHED
- EXISTING TREES TO REMAIN. REFER ALSO TO LANDSCAPE DRAWING.
- EXISTING TREES TO BE REMOVED. REFER ALSO TO LANDSCAPE DRAWING.

-PERFORM ALL THE DEMOLITION AS SHOWN ON THE DRAWING AND/OR AS NECESSARY REQUIRED CARRYING OUT THE WORKS UNDER THE CONTRACT.

-NB: CARE MUST BE TAKEN WHILE CARRING OUT THE WORKS.

-PROTECT EXISTING PROPERTY FROM DAMAGE BY APPROPRIATE MEANS INCLUDING SHORING, STRUTTING, PROTECTIVE SCREENS, SHEETING AND THE LIKE.

-REPAIR & REINSTATE ANY SUCH DAMAGE TO MATCH EXISTING.

-EXISTING SERVICES: DEAL AS APPROPRIATE WITH EXISTING SERVICES INCLUDED IN OR ENCOUNTERED DURING THE COURSE OF THE DEMOLITIONS.

-BEFORE DEMOLISHING AND REMOVING PARTS OF BUILDING HAVING ELECTRICAL WIRING, GAS, SEWER AND WATER PIPES, CONDUIT OR SIMILAR ITEMS EMBEDDED IN THEM, NOTIFY THE PROJECT MANAGER/ SUPERINTENDENT, AUTHORITIES HAVING JURISDICTION, AND MAKE SURE THAT THESE ITEMS ARE OUT OF SERVICE SO THAT THEY CAN BE REMOVED WITHOUT DANGER.

NOTES

- COMMON WALL FIRE SEPARATION CLAUSE 9.3.1 OF THE HOUSING PROVISIONS 2022 (FRL 60/60/60)
- COMMON WALL SOUND SEPARATION CLAUSE 10.7.1 OF THE HOUSING PROVISIONS 2022
- MECHANICAL VENTILATION CLAUSE 10.6.2 OF THE HOUSING PROVISIONS 2022
- SMOKE ALARMS CLAUSE 9.5.4 OF THE HOUSING PROVISIONS 2022
- BALUSTRADES INSTALLATION CLAUSE 11.3.4 OF THE HOUSING PROVISIONS 2022
- PROTECTION OF OPERABLE WINDOWS CLAUSE 11.3.7 OF THE HOUSING PROVISIONS 2022

LEGEND - WALL TYPES

- 250mm BRICK VENEER WALL
- 110mm FACE BRICK + 50mm CAVITY + 90mm TIMBER STUD + 10mm GYPROCK
- 230mm BRICK VENEER WALL
- 110mm FACE BRICK + 10mm CAVITY + 110mm FACE BRICK
- 90mm STUD WALL
- 10mm GYPROCK + 90mm TIMBER STUD + 10mm GYPROCK
- CSR 360 TIMBER FRAMED PARTY WALL SYSTEM
- 10mm GYPROCK + 90mm TIMBER STUD + 20mm CAVITY + 25mm GYPROCK SHAFT LINER PANEL + 90mm TIMBER STUD + 10mm GYPROCK
- 225mm HERAL VENEER WALL
- 10mm ACRYLIC RENDER + 100mm NRG
- Greenboard + 25mm CAVITY + 90mm TIMBER STUD + 10mm GYPROCK

01

ISSUE	DESCRIPTION	DATE
01	ISSUED FOR DA APPROVAL	9/05/2025
03	ISSUED FOR DA APPROVAL	8/08/2025
04	ISSUED FOR DA APPROVAL	22/10/2025
05	ISSUED FOR DA APPROVAL	7/11/2025
06	ISSUED FOR CC COORDINATION	2/03/2026
07	ISSUED FOR CC APPROVAL	4/05/2026


NOTES

The plans, drawings and specifications incorporated in this document shall remain the copyright © of ECOTECH DESIGNS PTY LTD and must not be used, reproduced or copied wholly or in part without prior written consent of ECOTECH DESIGNS PTY LTD.

Figured dimensions shall take preference over scaling. Verify all dimensions on site.

SCALE

1:100 @ A1 or 1:200 @ A3

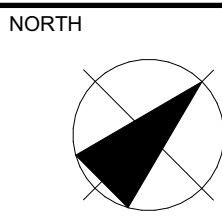

DRAWING TITLE

GROUND FLOOR PLAN


DRAWING NO

CC07

PROPOSED ATTACHED DUAL OCCUPANCY

26 MARSKELL CIRCUIT MUDGEE

JOB NO.	DATE	DRAWN	CHECKED	SCALE
25008	4/05/2026	P.G	P.G	As Shown on A1

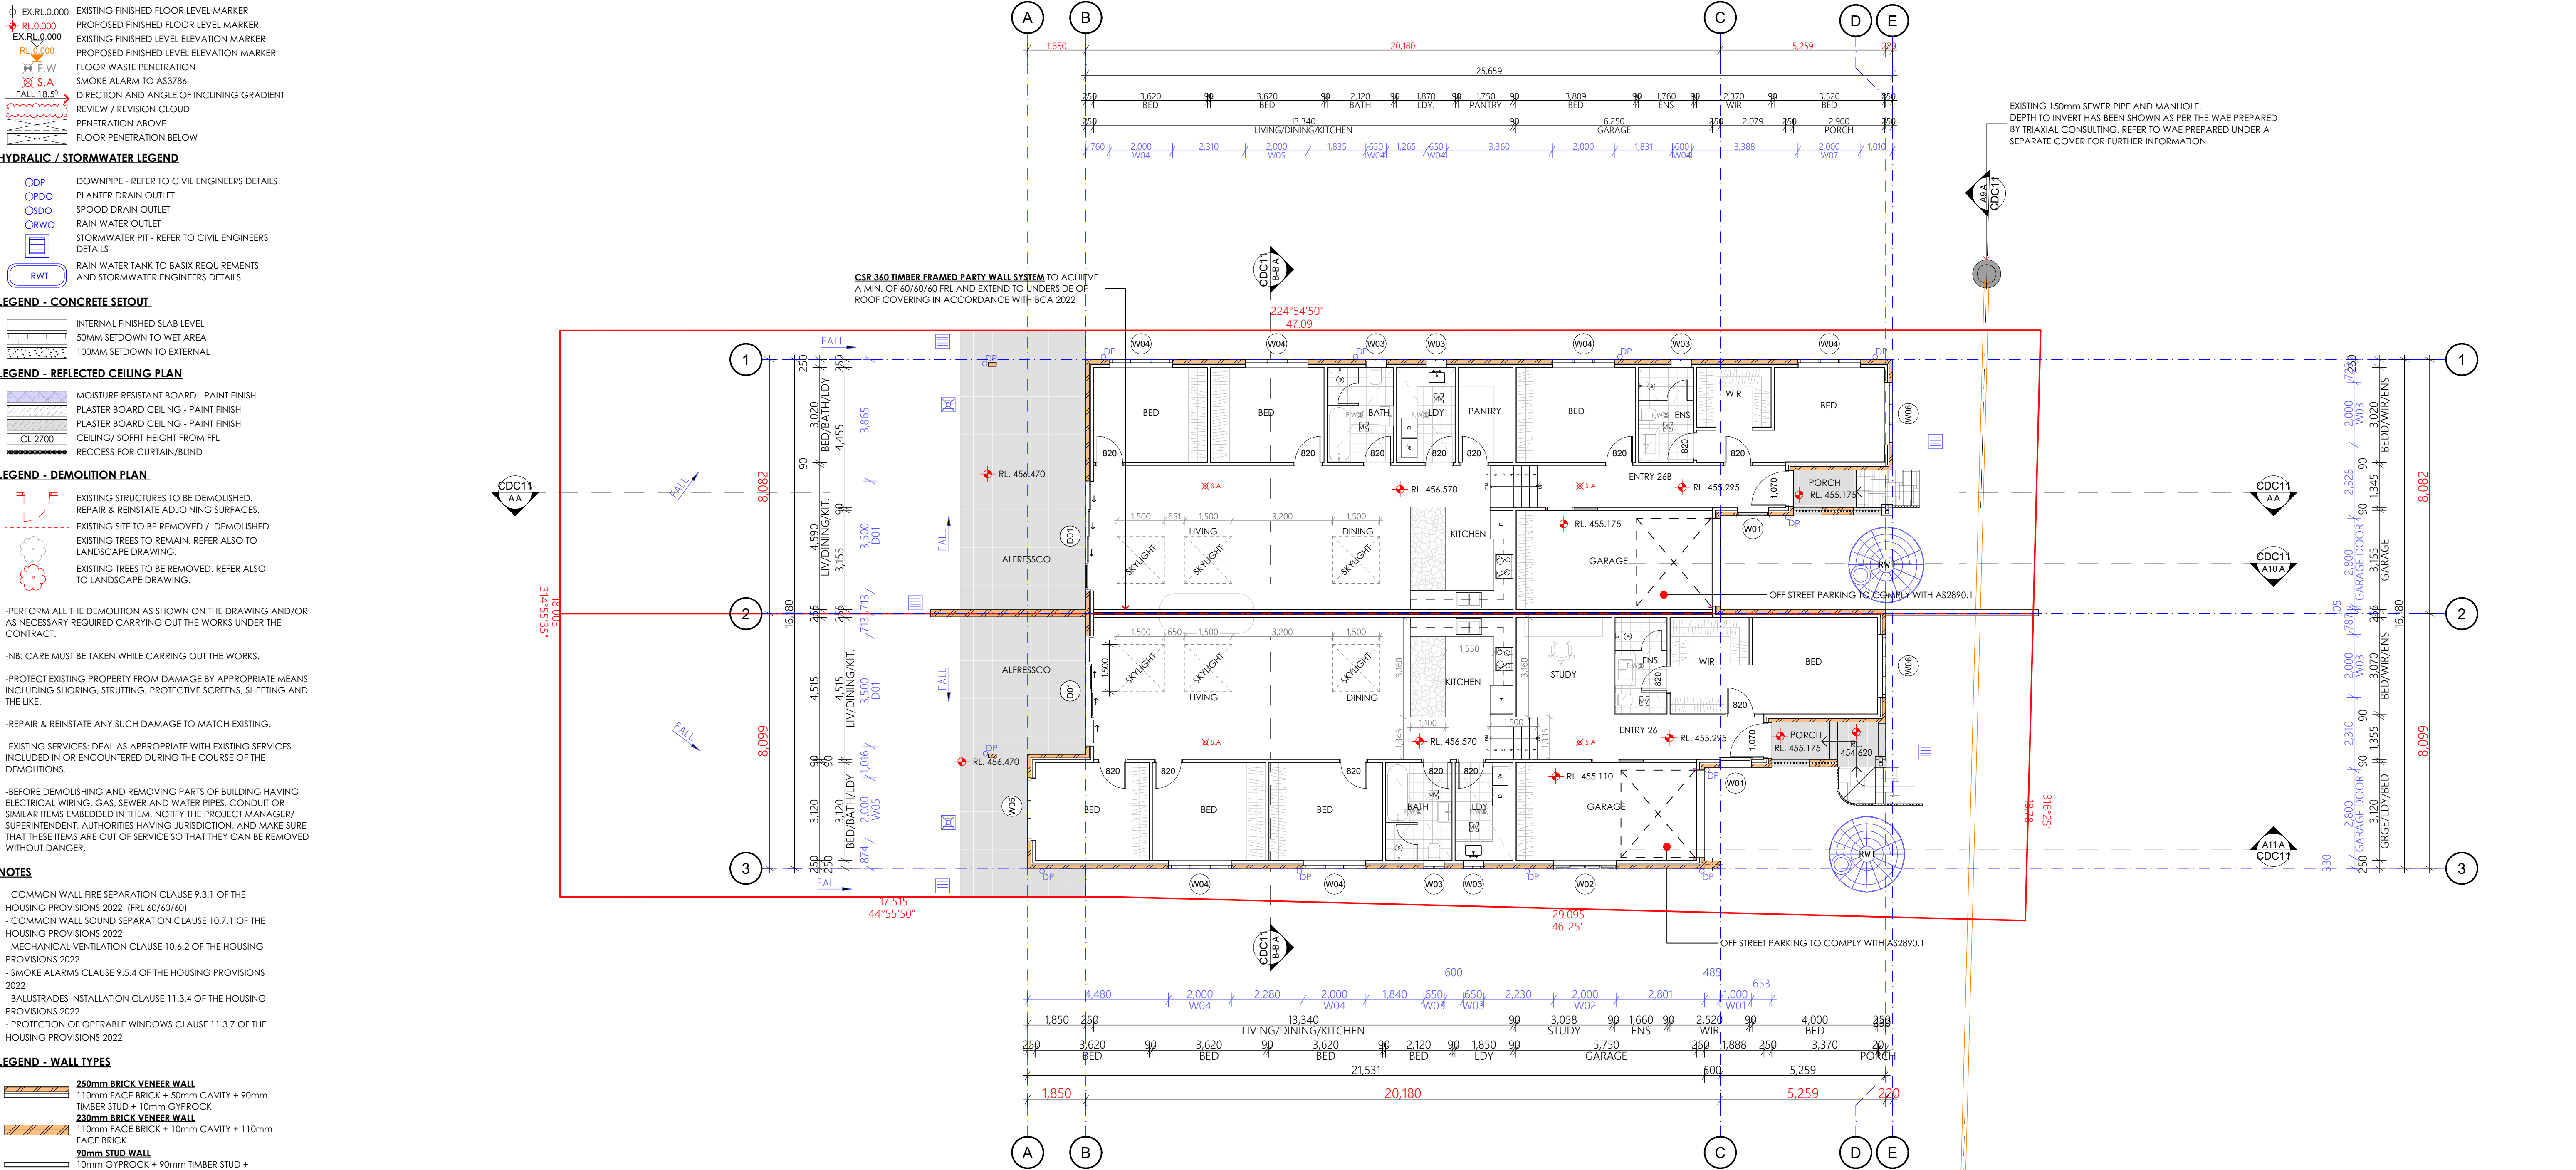

EXISTING 150mm SEWER PIPE AND MANHOLE. DEPTH TO INVERT HAS BEEN SHOWN AS PER THE WAE PREPARED BY TRIAXIAL CONSULTING. REFER TO WAE PREPARED UNDER A SEPARATE COVER FOR FURTHER INFORMATION

CSR 360 TIMBER FRAMED PARTY WALL SYSTEM TO ACHIEVE A MIN. OF 60/60/60 FRL AND EXTEND TO UNDERSIDE OF ROOF COVERING IN ACCORDANCE WITH BCA 2022

OFF STREET PARKING TO COMPLY WITH AS2890.1

OFF STREET PARKING TO COMPLY WITH AS2890.1

GROUND FLOOR

1:100

LEGEND - SITE PLAN

- EXTENT OF SITE BOUNDARY
- GRIDLINE
- STORMWATER PIT - REFER TO CIVIL ENGINEERS DETAILS
- DOWNPIPE - REFER TO CIVIL ENGINEERS DETAILS
- EXISTING SITE LEVELS
- PROPOSED TOP OF WALL LEVEL (TOW)
- PROPOSED BOTTOM OF WALL LEVEL (BOM)
- EXTERNAL LANDSCAPE AREA
- CONCRETE TO CIVIL ENGINEERS DETAILS

LEGEND - SUBDIVISION PLAN

- PROPOSED LINE OF SUBDIVISION
- PROPOSED BUILDING FOOTPRINT
- SITE AREA CALCULATION

LEGEND - GFA & CALCULATIONS

- GROSS FLOOR AREA (GFA)
- LANDSCAPING AREA (MIN. 1.5x1.5m)
- PRIVATE OPEN SPACE (MIN. 4x4m)
- ARTICULATION ZONE (1.5m)
- ARTICULATION ELEMENTS (25%)

GENERAL LEGEND

- EXISTING FINISHED FLOOR LEVEL MARKER
- PROPOSED FINISHED FLOOR LEVEL MARKER
- EXISTING FINISHED LEVEL ELEVATION MARKER
- PROPOSED FINISHED LEVEL ELEVATION MARKER
- FLOOR WASTE PENETRATION
- SMOKE ALARM TO AS3786
- DIRECTION AND ANGLE OF INCLINING GRADIENT
- REVIEW / REVISION CLOUD
- PENETRATION ABOVE
- FLOOR PENETRATION BELOW

HYDRAULIC / STORMWATER LEGEND

- DOWNPIPE - REFER TO CIVIL ENGINEERS DETAILS
- PLANTER DRAIN OUTLET
- SPOOD DRAIN OUTLET
- RAIN WATER OUTLET
- STORMWATER PIT - REFER TO CIVIL ENGINEERS DETAILS
- RAIN WATER TANK TO BASIX REQUIREMENTS AND STORMWATER ENGINEERS DETAILS

LEGEND - CONCRETE SETOUT

- INTERNAL FINISHED SLAB LEVEL
- 50MM SETDOWN TO WET AREA
- 100MM SETDOWN TO EXTERNAL

LEGEND - REFLECTED CEILING PLAN

- MOISTURE RESISTANT BOARD - PAINT FINISH
- PLASTER BOARD CEILING - PAINT FINISH
- PLASTER BOARD CEILING - PAINT FINISH
- CEILING/ SOFFIT HEIGHT FROM FFL
- RECESS FOR CURTAIN/BLIND

LEGEND - DEMOLITION PLAN

- EXISTING STRUCTURES TO BE DEMOLISHED. REPAIR & REINSTATE ADJOINING SURFACES.
- EXISTING SITE TO BE REMOVED / DEMOLISHED
- EXISTING TREES TO REMAIN. REFER ALSO TO LANDSCAPE DRAWING.
- EXISTING TREES TO BE REMOVED. REFER ALSO TO LANDSCAPE DRAWING.

-PERFORM ALL THE DEMOLITION AS SHOWN ON THE DRAWING AND/OR AS NECESSARY REQUIRED CARRYING OUT THE WORKS UNDER THE CONTRACT.

-NB: CARE MUST BE TAKEN WHILE CARRING OUT THE WORKS.

-PROTECT EXISTING PROPERTY FROM DAMAGE BY APPROPRIATE MEANS INCLUDING SHORING, STRUTTING, PROTECTIVE SCREENS, SHEETING AND THE LIKE.

-REPAIR & REINSTATE ANY SUCH DAMAGE TO MATCH EXISTING.

-EXISTING SERVICES: DEAL AS APPROPRIATE WITH EXISTING SERVICES INCLUDED IN OR ENCOUNTERED DURING THE COURSE OF THE DEMOLITIONS.

-BEFORE DEMOLISHING AND REMOVING PARTS OF BUILDING HAVING ELECTRICAL WIRING, GAS, SEWER AND WATER PIPES, CONDUIT OR SIMILAR ITEMS EMBEDDED IN THEM, NOTIFY THE PROJECT MANAGER/ SUPERINTENDENT, AUTHORITIES HAVING JURISDICTION, AND MAKE SURE THAT THESE ITEMS ARE OUT OF SERVICE SO THAT THEY CAN BE REMOVED WITHOUT DANGER.


NOTES

- COMMON WALL FIRE SEPARATION CLAUSE 9.3.1 OF THE HOUSING PROVISIONS 2022 (FRL 60/60/60)
- COMMON WALL SOUND SEPARATION CLAUSE 10.7.1 OF THE HOUSING PROVISIONS 2022
- MECHANICAL VENTILATION CLAUSE 10.6.2 OF THE HOUSING PROVISIONS 2022
- SMOKE ALARMS CLAUSE 9.5.4 OF THE HOUSING PROVISIONS 2022
- BALUSTRADES INSTALLATION CLAUSE 11.3.4 OF THE HOUSING PROVISIONS 2022
- PROTECTION OF OPERABLE WINDOWS CLAUSE 11.3.7 OF THE HOUSING PROVISIONS 2022

LEGEND - WALL TYPES

- 250mm BRICK VENEER WALL
- 110mm FACE BRICK + 50mm CAVITY + 90mm TIMBER STUD + 10mm GYPROCK
- 230mm BRICK VENEER WALL
- 110mm FACE BRICK + 10mm CAVITY + 110mm FACE BRICK
- 90mm STUD WALL
- 10mm GYPROCK + 90mm TIMBER STUD + 10mm GYPROCK
- CSR 360 TIMBER FRAMED PARTY WALL SYSTEM
- 10mm GYPROCK + 90mm TIMBER STUD + 20mm CAVITY + 25mm GYPROCK SHAFT LINER PANEL + 90mm TIMBER STUD + 10mm GYPROCK
- 225mm HERAL VENEER WALL
- 10mm ACRYLIC RENDER + 100mm NRG
- Greenboard + 25mm CAVITY + 90mm TIMBER STUD + 10mm GYPROCK

01

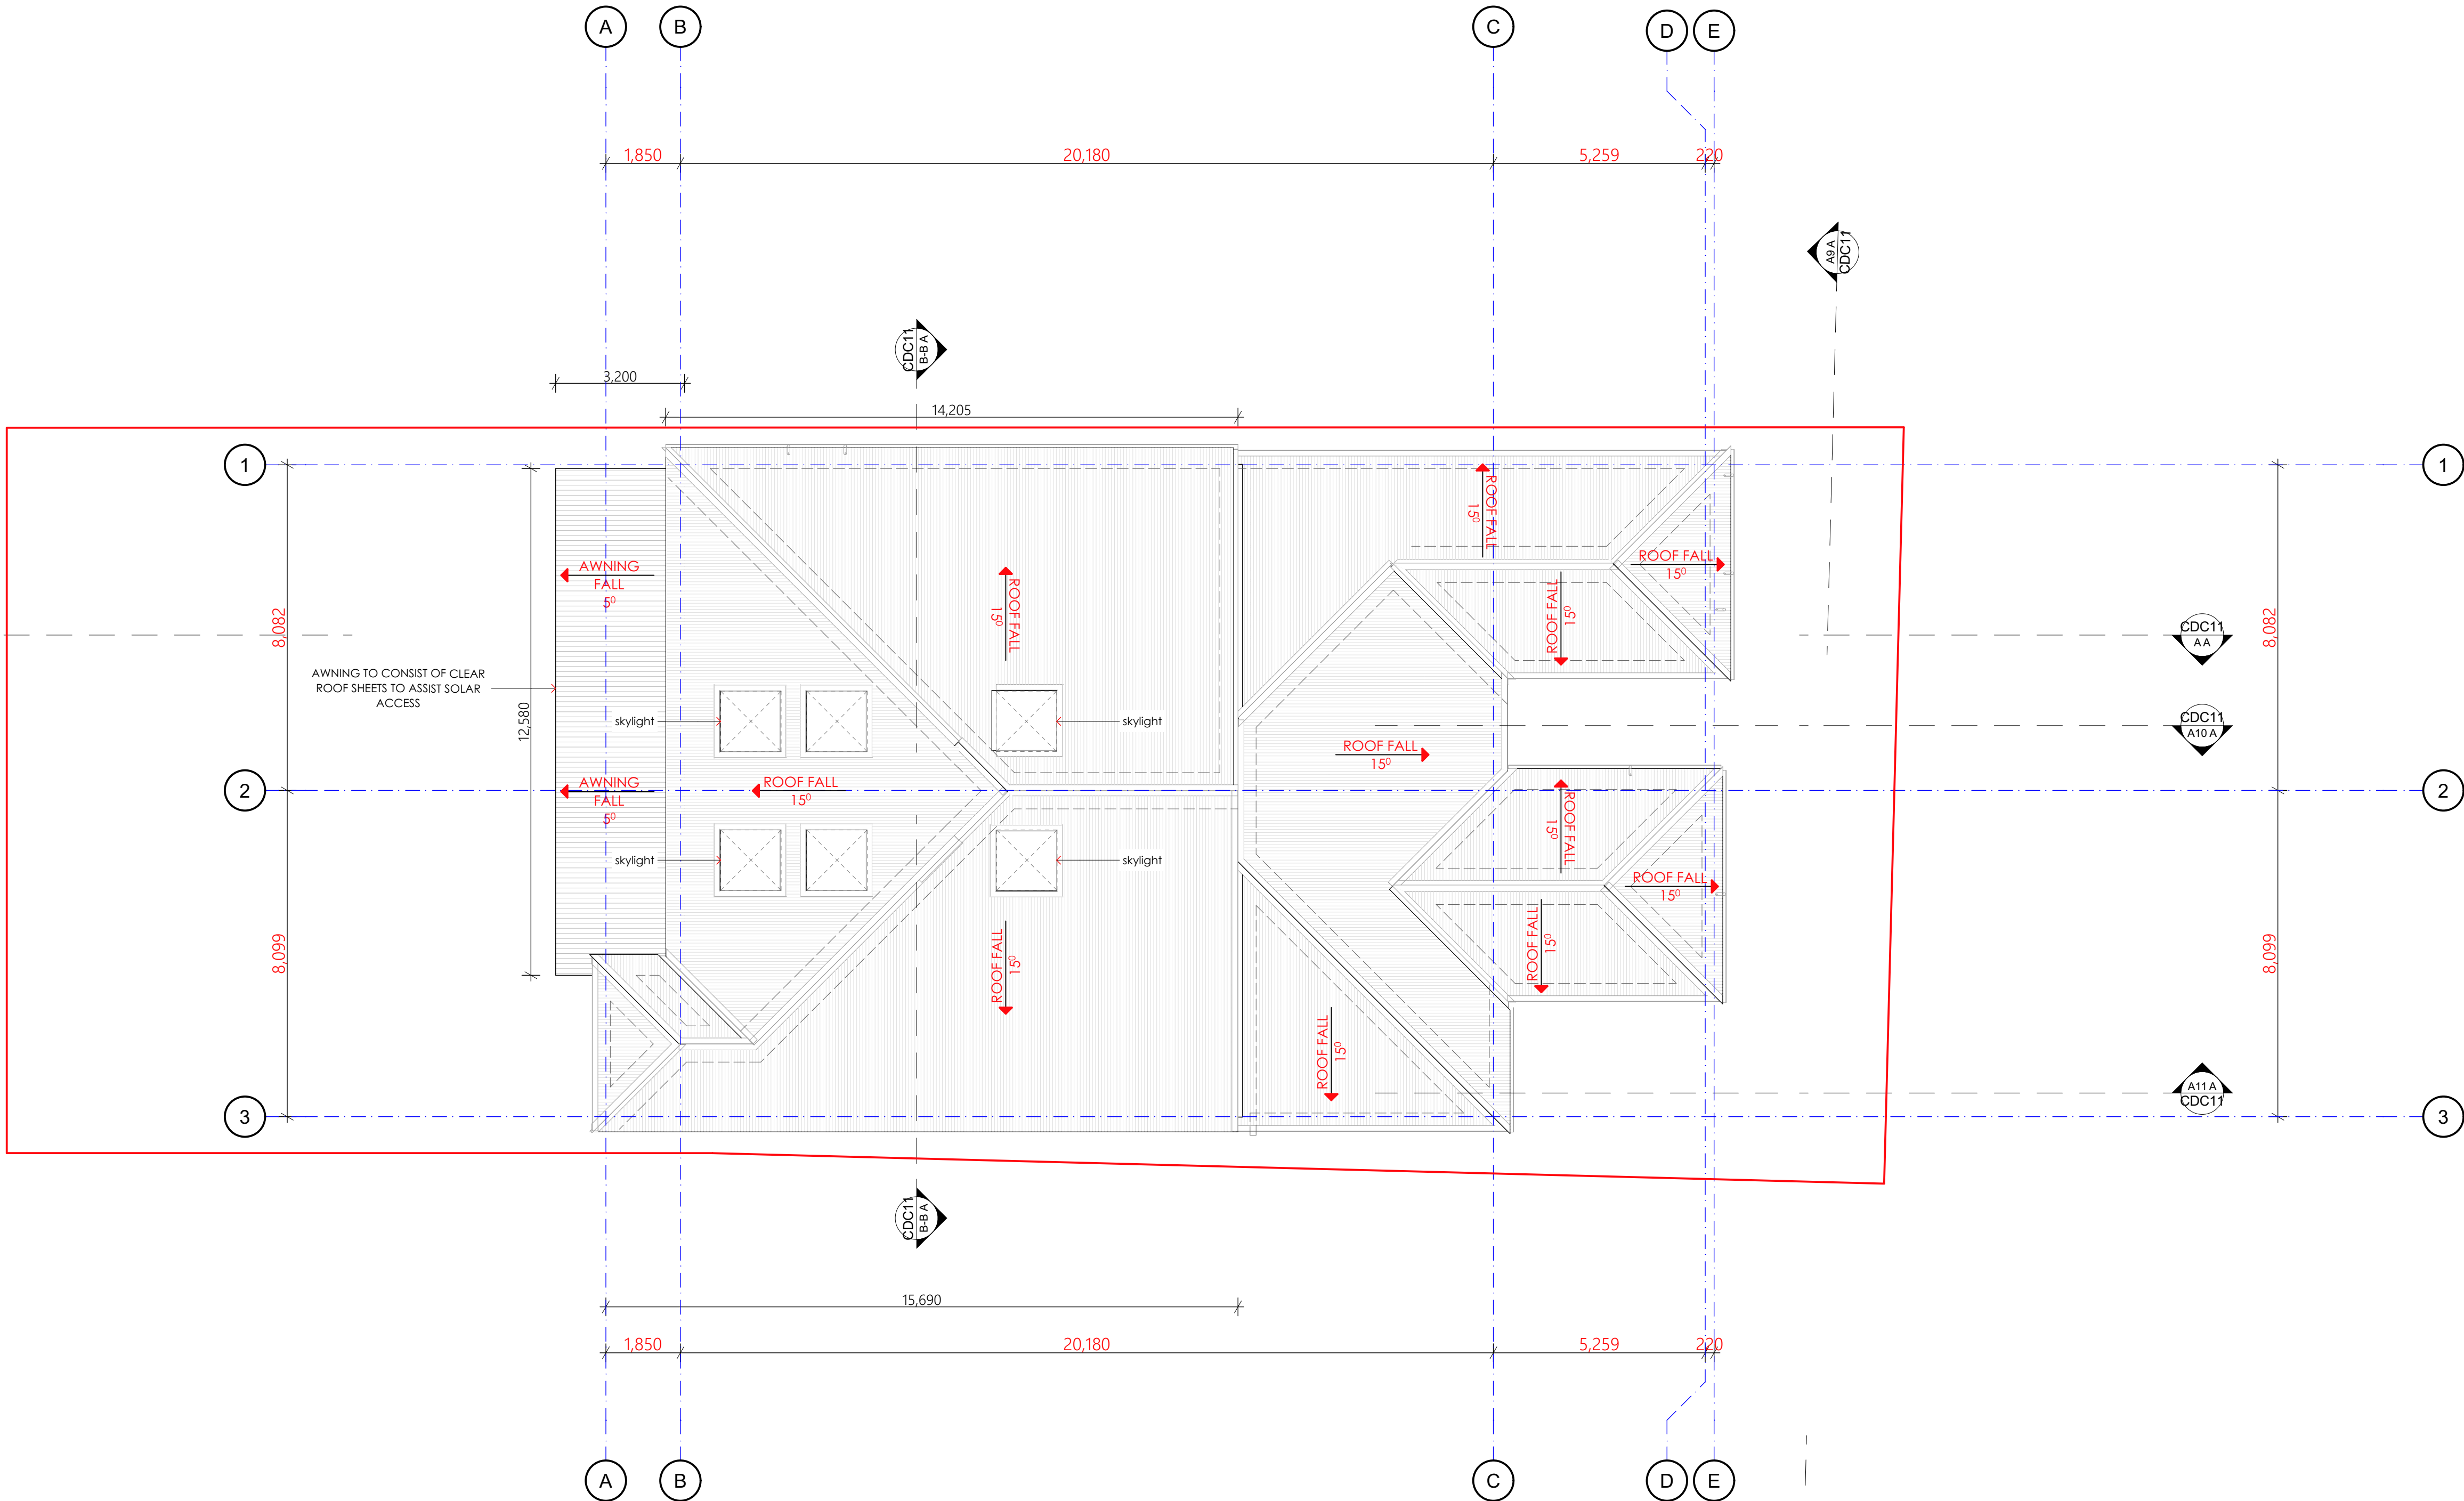

ROOF PLAN
1:100

ISSUE	DESCRIPTION	DATE	NOTES	SCALE	NORTH	DRAWING TITLE	PROPOSED ATTACHED DUAL OCCUPANCY 26 MARSKELL CIRCUIT MUDGEE					 ECOTECH DESIGNS BUILDING DREAMS SUSTAINABLY				
01	ISSUED FOR DA APPROVAL	9/05/2025	The plans, drawings and specifications incorporated in this document shall remain the copyright © of ECOTECH DESIGNS PTY LTD and must not be used, reproduced or copied wholly or in part without prior written consent of ECOTECH DESIGNS PTY LTD. Figured dimensions shall take preference over scaling. Verify all dimensions on site.	1:100 @ A1 or 1:200 @ A3		ROOF PLAN DRAWING NO CC08										
03	ISSUED FOR DA APPROVAL	8/08/2025														
04	ISSUED FOR DA APPROVAL	22/10/2025														
05	ISSUED FOR DA APPROVAL	7/11/2025														
06	ISSUED FOR CC COORDINATION	2/03/2026														
07	ISSUED FOR CC APPROVAL	4/05/2026														
							JOB NO. 25008	DATE 4/05/2026	DRAWN P.G	CHECKED P.G	SCALE As Shown on A1					

LEGEND - SITE PLAN

- EXTENT OF SITE BOUNDARY
- GRIDLINE
- STORMWATER PIT - REFER TO CIVIL ENGINEERS DETAILS
- DOWNPIPE - REFER TO CIVIL ENGINEERS DETAILS
- EXISTING SITE LEVELS
- PROPOSED TOP OF WALL LEVEL (TOW)
- PROPOSED BOTTOM OF WALL LEVEL (BOM)
- EXTERNAL LANDSCAPE AREA
- CONCRETE TO CIVIL ENGINEERS DETAILS

LEGEND - SUBDIVISION PLAN

- PROPOSED LINE OF SUBDIVISION
- PROPOSED BUILDING FOOTPRINT
- SITE AREA CALCULATION

LEGEND - GFA & CALCULATIONS

- GROSS FLOOR AREA (GFA)
- LANDSCAPING AREA (MIN. 1.5x1.5m)
- PRIVATE OPEN SPACE (MIN. 4x4m)
- ARTICULATION ZONE (1.5m)
- ARTICULATION ELEMENTS (25%)

GENERAL LEGEND

- EXISTING FINISHED FLOOR LEVEL MARKER
- PROPOSED FINISHED FLOOR LEVEL MARKER
- EXISTING FINISHED LEVEL ELEVATION MARKER
- PROPOSED FINISHED LEVEL ELEVATION MARKER
- FLOOR WASTE PENETRATION
- SMOKE ALARM TO AS3786
- DIRECTION AND ANGLE OF INCLINING GRADIENT
- REVIEW / REVISION CLOUD
- PENETRATION ABOVE
- FLOOR PENETRATION BELOW

HYDRAULIC / STORMWATER LEGEND

- DOWNPIPE - REFER TO CIVIL ENGINEERS DETAILS
- PLANTER DRAIN OUTLET
- SPOOD DRAIN OUTLET
- RAIN WATER OUTLET
- STORMWATER PIT - REFER TO CIVIL ENGINEERS DETAILS
- RAIN WATER TANK TO BASIX REQUIREMENTS AND STORMWATER ENGINEERS DETAILS

LEGEND - CONCRETE SETOUT

- INTERNAL FINISHED SLAB LEVEL
- 50MM SETDOWN TO WET AREA
- 100MM SETDOWN TO EXTERNAL

LEGEND - REFLECTED CEILING PLAN

- MOISTURE RESISTANT BOARD - PAINT FINISH
- PLASTER BOARD CEILING - PAINT FINISH
- PLASTER BOARD CEILING - PAINT FINISH
- CEILING/ SOFFIT HEIGHT FROM FFL
- RECESS FOR CURTAIN/BLIND

LEGEND - DEMOLITION PLAN

- EXISTING STRUCTURES TO BE DEMOLISHED. REPAIR & REINSTATE ADJOINING SURFACES.
- EXISTING SITE TO BE REMOVED / DEMOLISHED
- EXISTING TREES TO REMAIN. REFER ALSO TO LANDSCAPE DRAWING.
- EXISTING TREES TO BE REMOVED. REFER ALSO TO LANDSCAPE DRAWING.

-PERFORM ALL THE DEMOLITION AS SHOWN ON THE DRAWING AND/OR AS NECESSARY REQUIRED CARRYING OUT THE WORKS UNDER THE CONTRACT.

-NB: CARE MUST BE TAKEN WHILE CARRING OUT THE WORKS.

-PROTECT EXISTING PROPERTY FROM DAMAGE BY APPROPRIATE MEANS INCLUDING SHORING, STRUTTING, PROTECTIVE SCREENS, SHEETING AND THE LIKE.

-REPAIR & REINSTATE ANY SUCH DAMAGE TO MATCH EXISTING.

-EXISTING SERVICES: DEAL AS APPROPRIATE WITH EXISTING SERVICES INCLUDED IN OR ENCOUNTERED DURING THE COURSE OF THE DEMOLITIONS.





-BEFORE DEMOLISHING AND REMOVING PARTS OF BUILDING HAVING ELECTRICAL WIRING, GAS, SEWER AND WATER PIPES, CONDUIT OR SIMILAR ITEMS EMBEDDED IN THEM, NOTIFY THE PROJECT MANAGER/ SUPERINTENDENT, AUTHORITIES HAVING JURISDICTION, AND MAKE SURE THAT THESE ITEMS ARE OUT OF SERVICE SO THAT THEY CAN BE REMOVED WITHOUT DANGER.

NOTES

- COMMON WALL FIRE SEPARATION CLAUSE 9.3.1 OF THE HOUSING PROVISIONS 2022 (FRL 60/60/60)
- COMMON WALL SOUND SEPARATION CLAUSE 10.7.1 OF THE HOUSING PROVISIONS 2022
- MECHANICAL VENTILATION CLAUSE 10.6.2 OF THE HOUSING PROVISIONS 2022
- SMOKE ALARMS CLAUSE 9.5.4 OF THE HOUSING PROVISIONS 2022
- BALUSTRADES INSTALLATION CLAUSE 11.3.4 OF THE HOUSING PROVISIONS 2022
- PROTECTION OF OPERABLE WINDOWS CLAUSE 11.3.7 OF THE HOUSING PROVISIONS 2022


LEGEND - WALL TYPES

- 250mm BRICK VENEER WALL
- 110mm FACE BRICK + 50mm CAVITY + 90mm TIMBER STUD + 10mm GYPROCK
- 230mm BRICK VENEER WALL
- 110mm FACE BRICK + 10mm CAVITY + 110mm FACE BRICK
- 90mm STUD WALL
- 10mm GYPROCK + 90mm TIMBER STUD + 10mm GYPROCK
- CSR 360 TIMBER FRAMED PARTY WALL SYSTEM
- 10mm GYPROCK + 90mm TIMBER STUD + 20mm CAVITY + 25mm GYPROCK SHAFT LINER PANEL + 90mm TIMBER STUD + 10mm GYPROCK
- 225mm HERBAL VENEER WALL
- 10mm ACRYLIC RENDER + 100mm NRG
- Greenboard + 25mm CAVITY + 90mm TIMBER STUD + 10mm GYPROCK

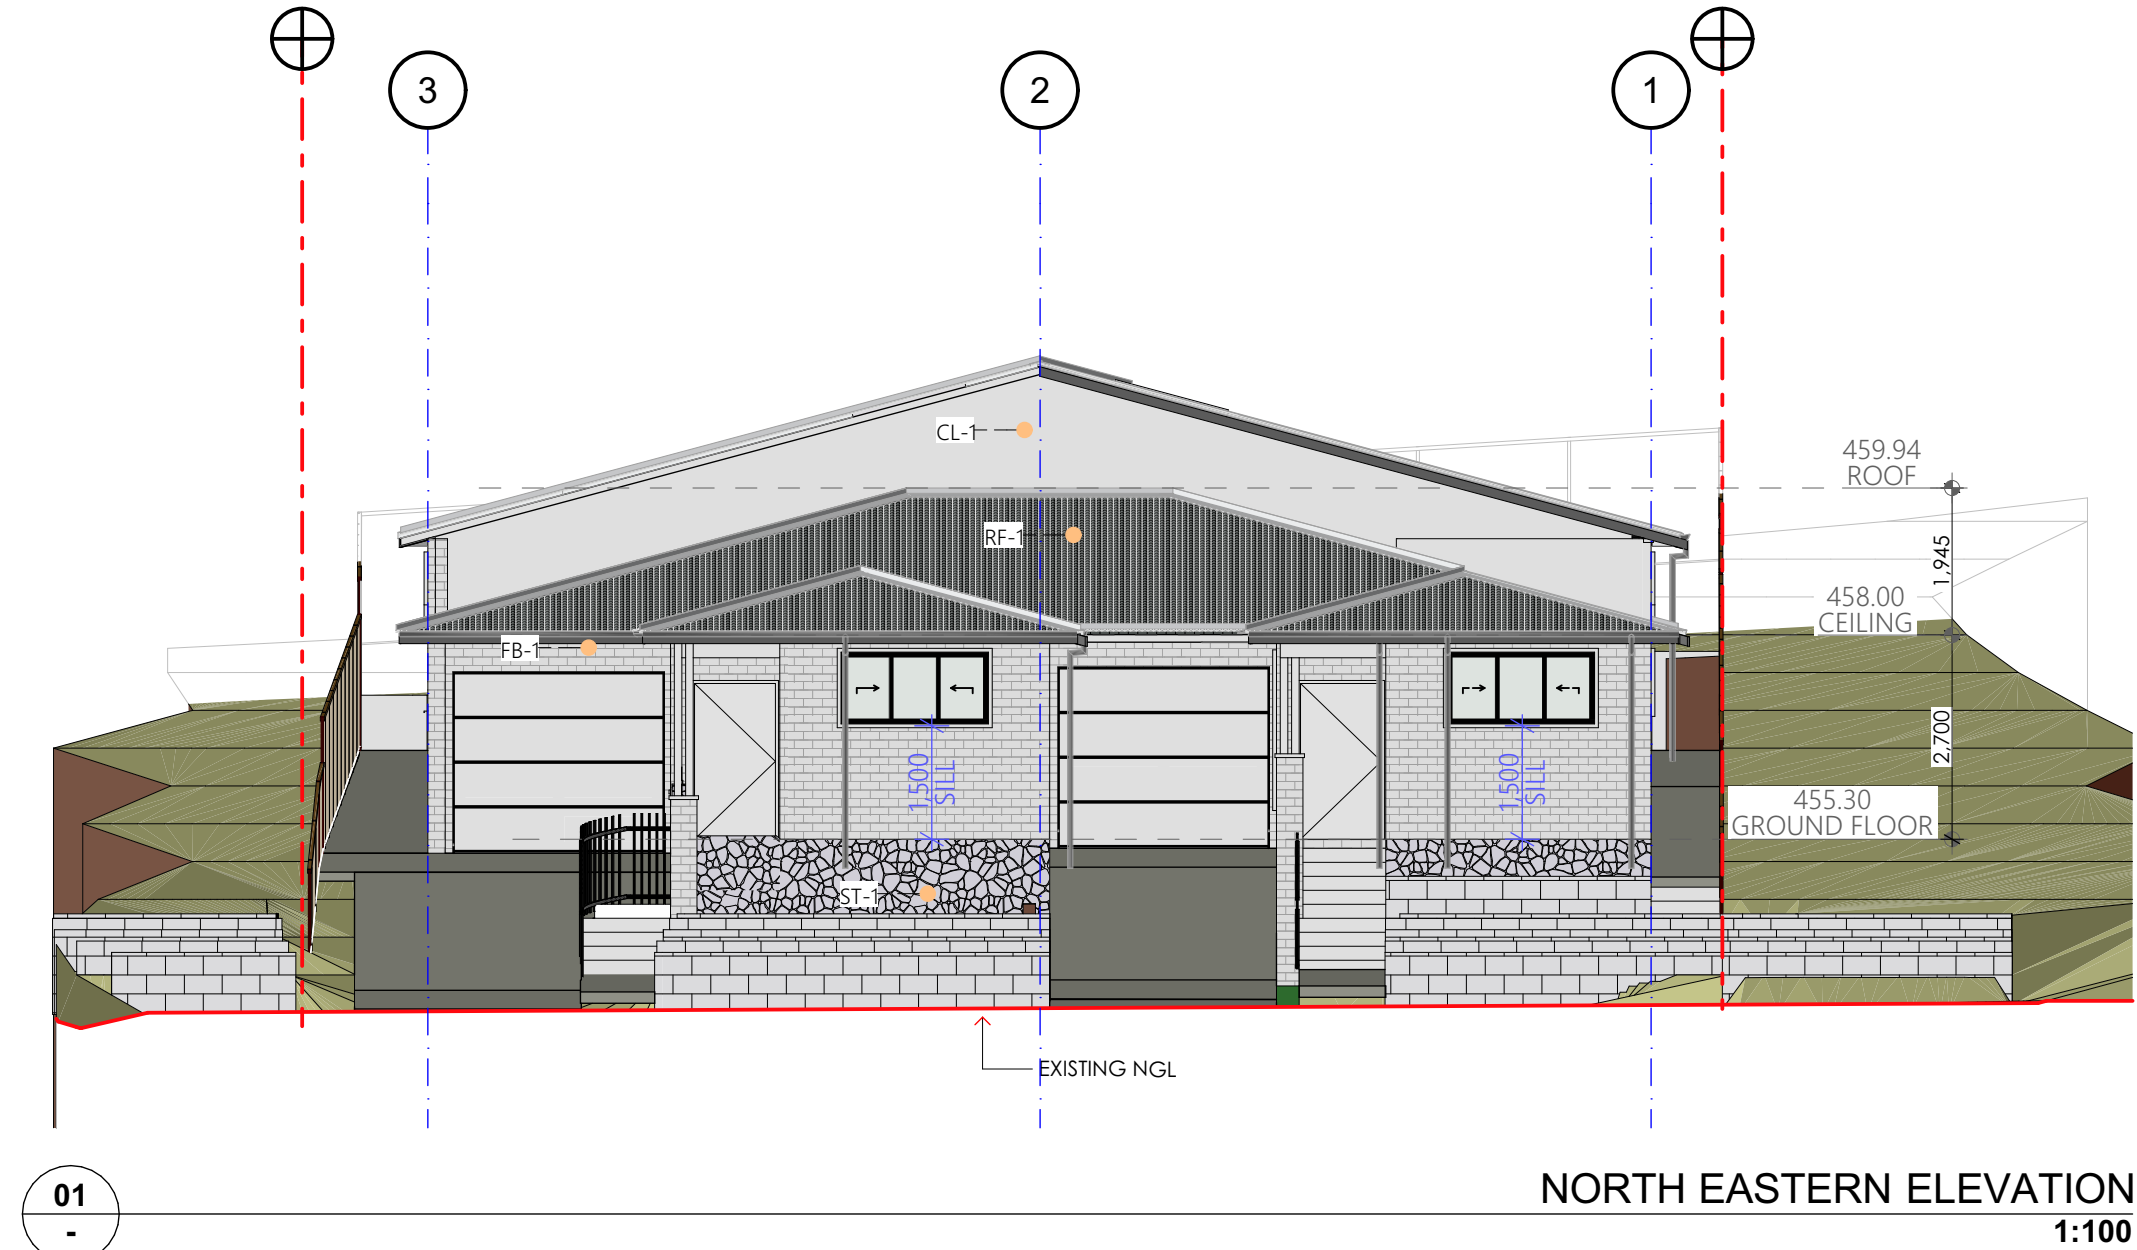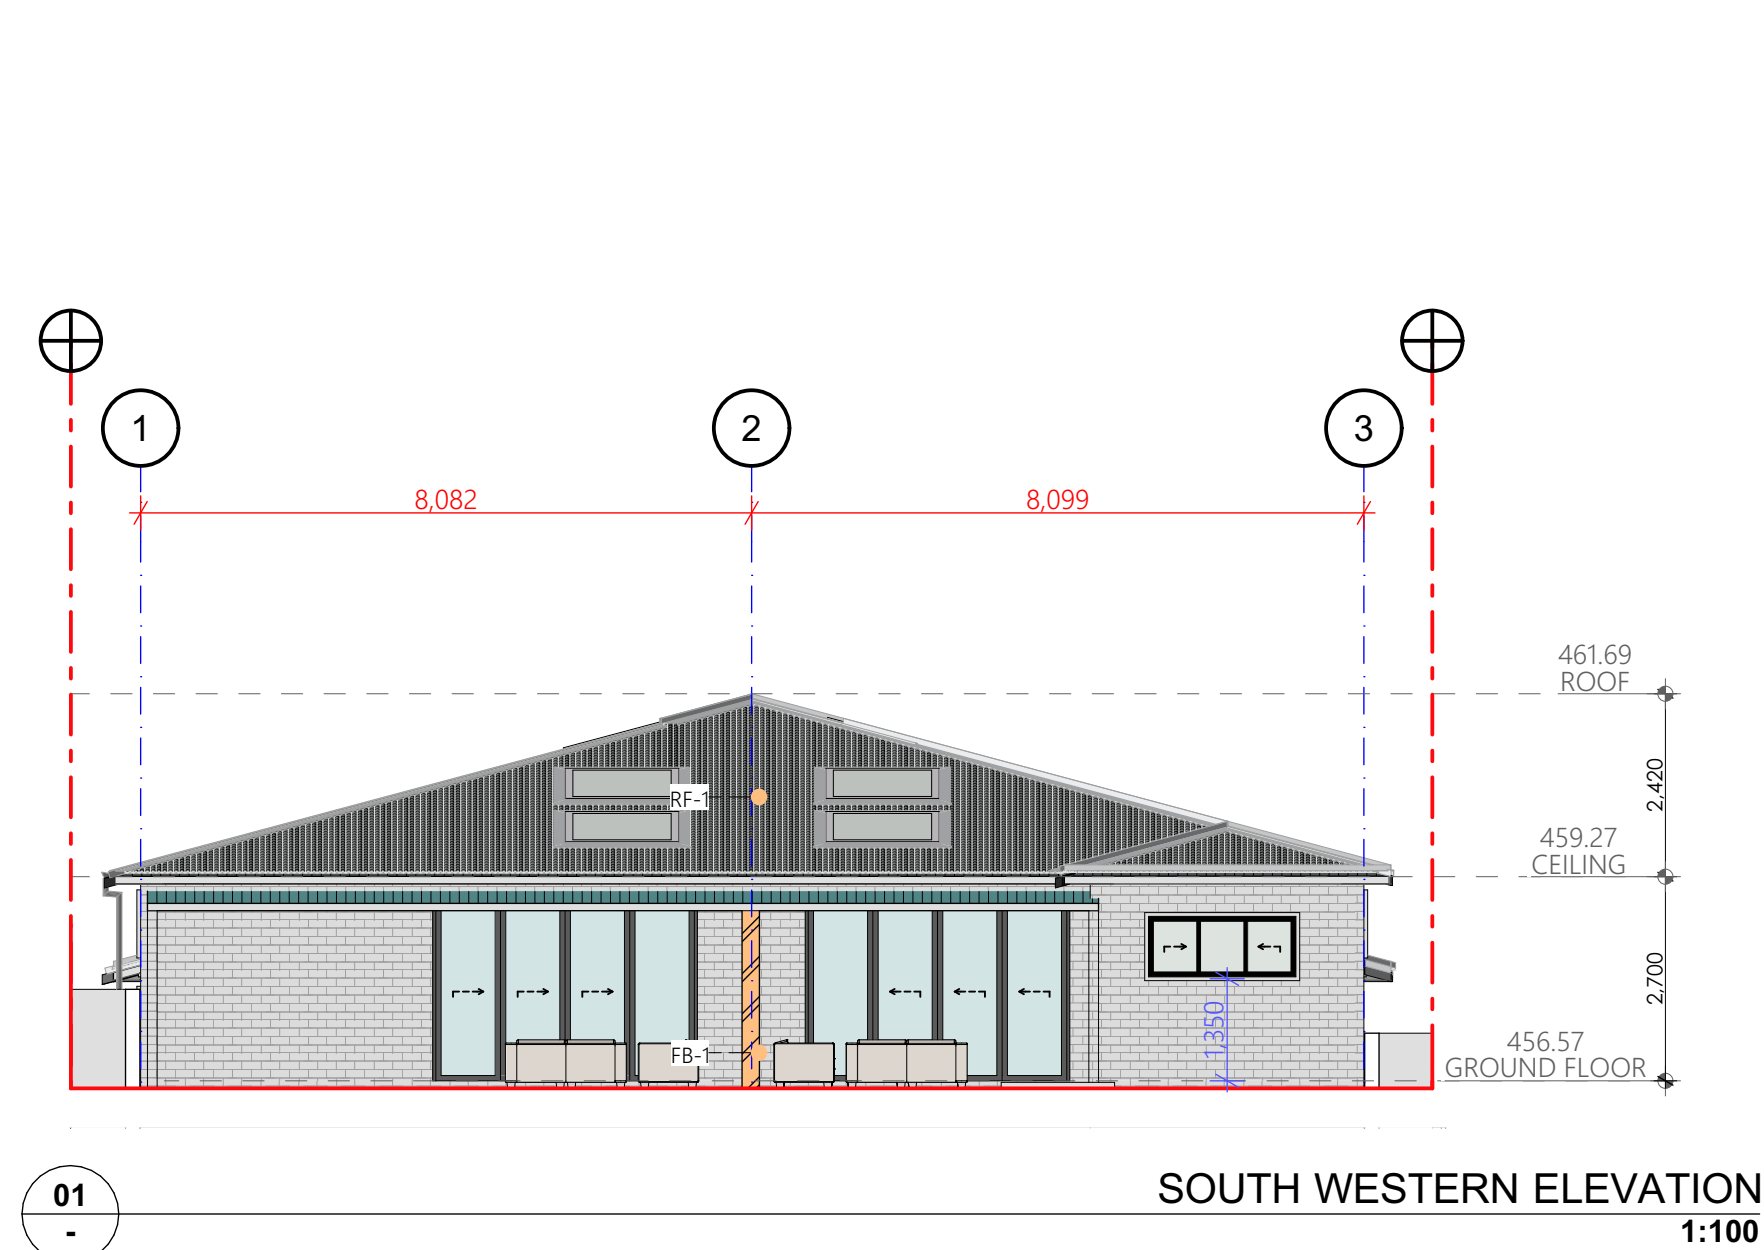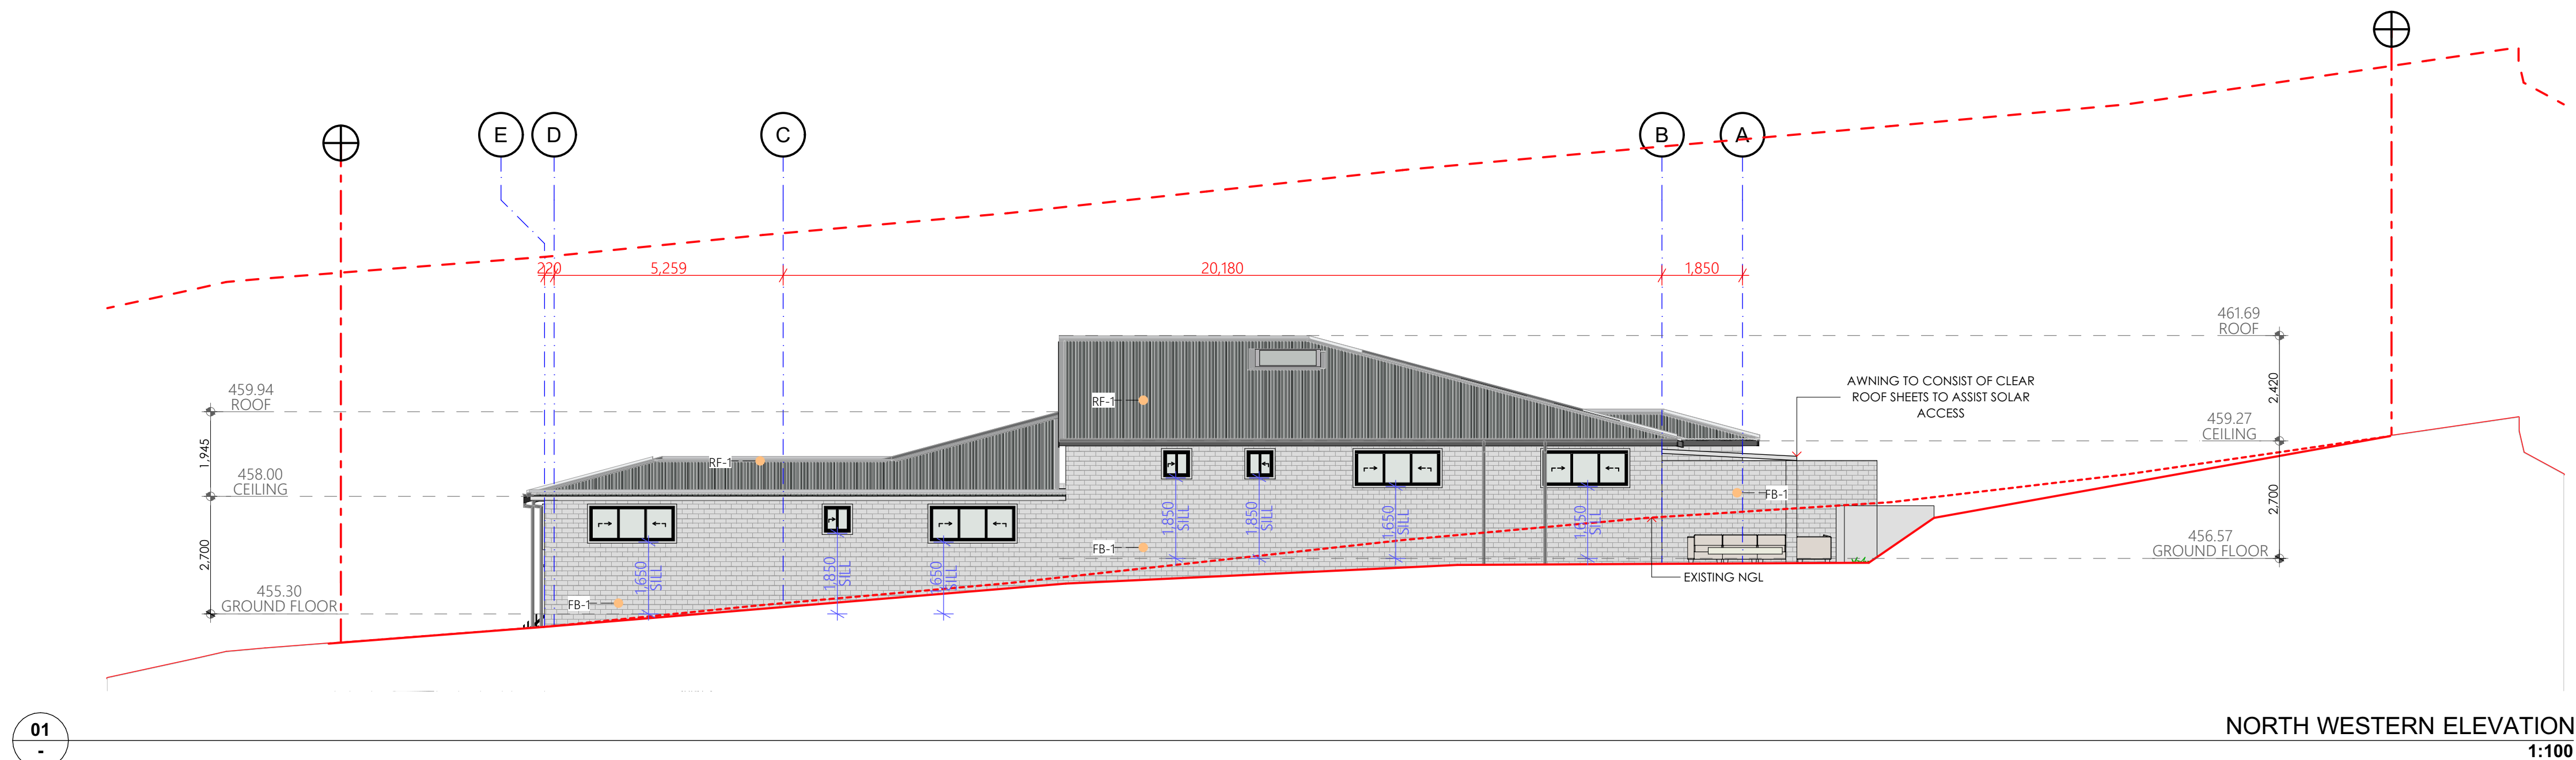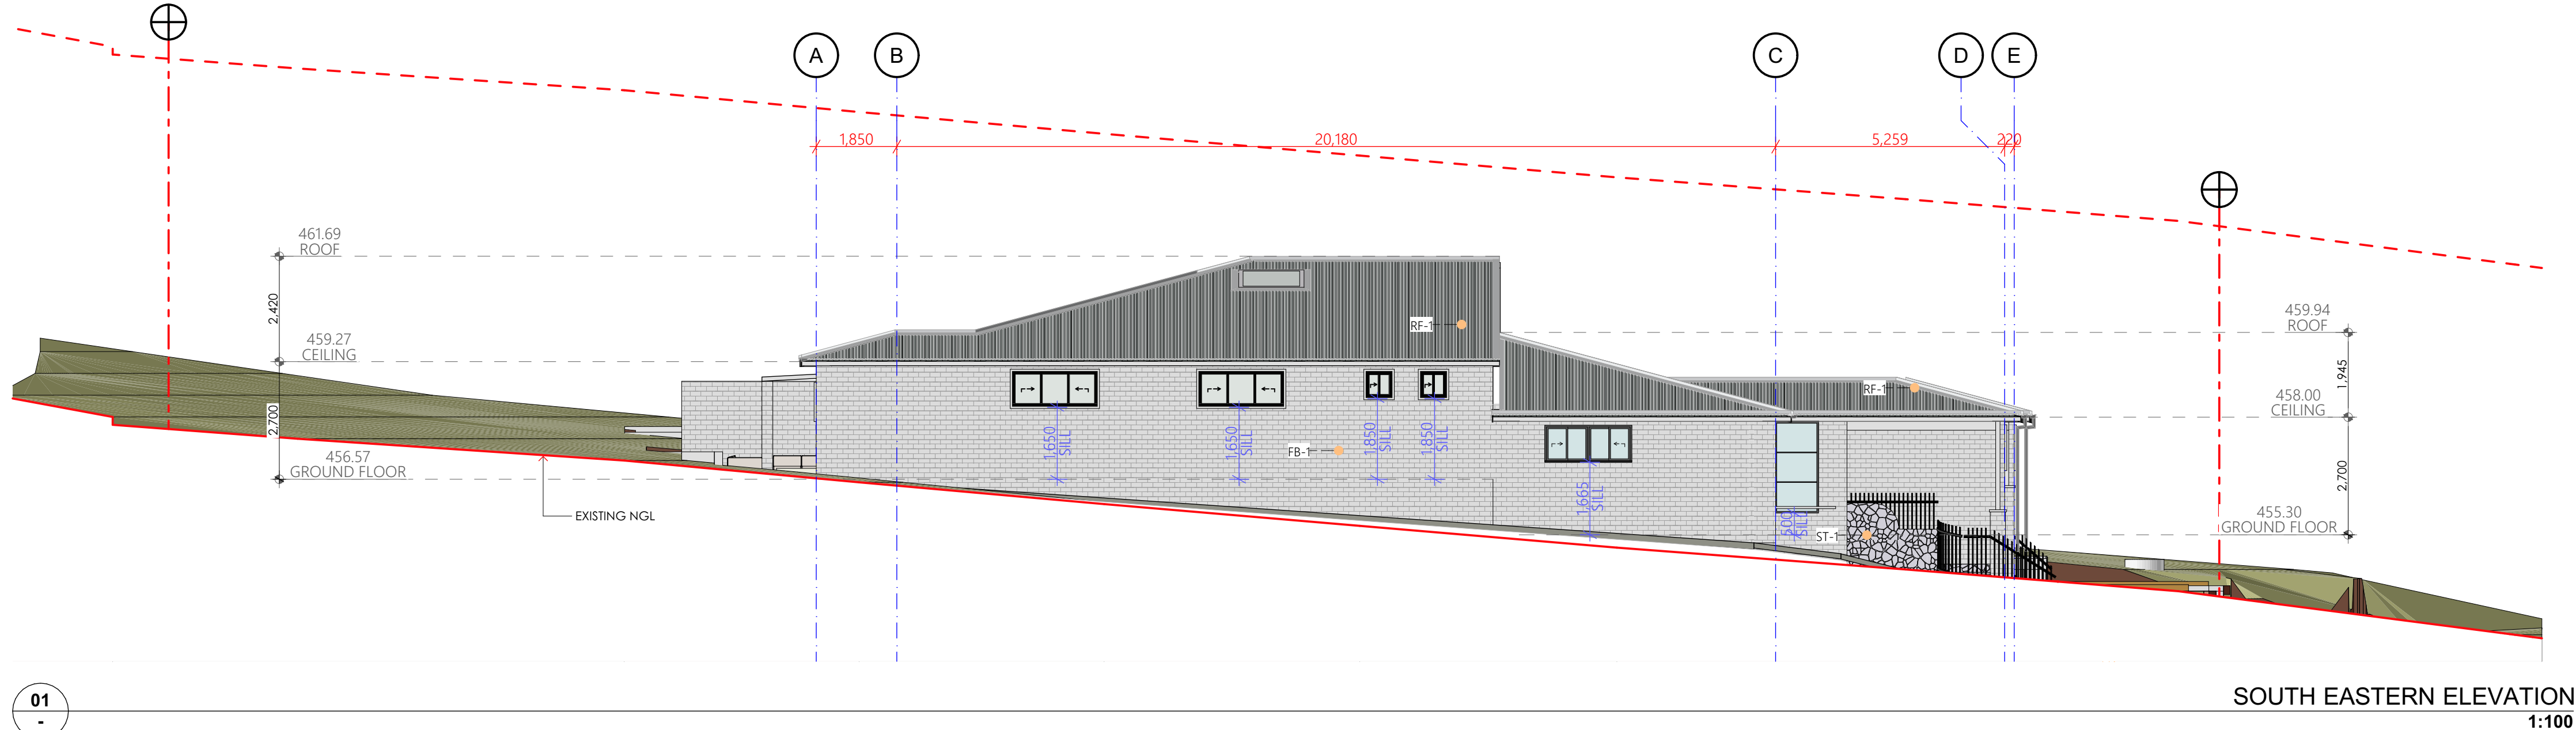

SCHEDULE OF EXTERNAL MATERIAL & FINISHES:

PT-1: CEMENT RENDER - PAINT
FINISH - DULUX LEXICON
QUARTER OR SIMILIAR

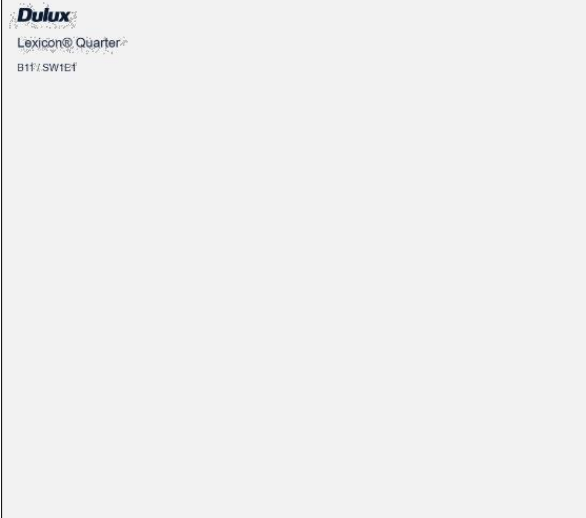

EXTERNAL WINDOW FRAMES
PAINTED DULUX MONUMENT
GREY




FB-1: PGH MORADA CENIZA
OR SIMILIAR



ST-1:
STONE FEATURE WALL
QUARTER OR SIMILIAR



COLOURBOND PALE
EUCALYPT FENCE

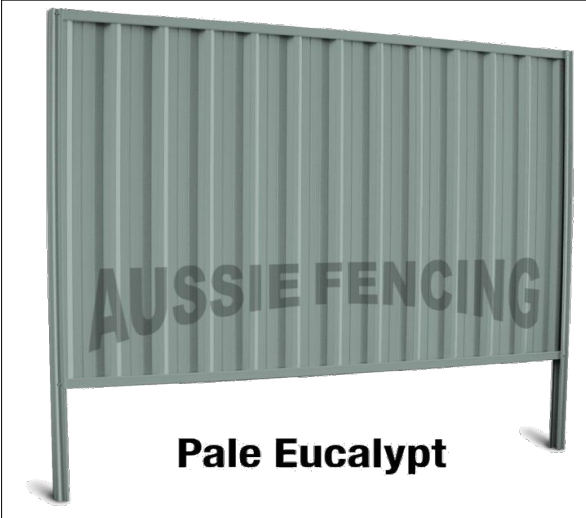

ISSUE	DESCRIPTION	DATE	NOTES	SCALE	NORTH	DRAWING TITLE	PROPOSED ATTACHED DUAL OCCUPANCY 26 MARSKELL CIRCUIT MUDGE					 ECOTECH DESIGNS BUILDING DREAMS SUSTAINABLY
01	ISSUED FOR DA APPROVAL	9/05/2025	The plans, drawings and specifications incorporated in this document shall remain the copyright © of ECOTECH DESIGNS PTY LTD and must not be used, reproduced or copied wholly or in part without prior written consent of ECOTECH DESIGNS PTY LTD. Figured dimensions shall take preference over scaling. Verify all dimensions on site.	1:100 @ A1 or 1:200 @ A3		ELEVATIONS DRAWING NO CC09						
03	ISSUED FOR DA APPROVAL	8/08/2025										
04	ISSUED FOR DA APPROVAL	22/10/2025										
05	ISSUED FOR DA APPROVAL	7/11/2025										
06	ISSUED FOR CC COORDINATRION	2/03/2026										
07	ISSUED FOR CC APPROVAL	4/05/2026										
							JOB NO. 25008	DATE 4/05/2026	DRAWN P.G	CHECKED P.G	SCALE As Shown on A1	

LEGEND - SITE PLAN

- EXTENT OF SITE BOUNDARY
- GRIDLINE
- STORMWATER PIT - REFER TO CIVIL ENGINEERS DETAILS
- DOWNPIPE - REFER TO CIVIL ENGINEERS DETAILS
- EXISTING SITE LEVELS
- PROPOSED TOP OF WALL LEVEL (TOW)
- PROPOSED BOTTOM OF WALL LEVEL (BOM)
- EXTERNAL LANDSCAPE AREA
- CONCRETE TO CIVIL ENGINEERS DETAILS

LEGEND - SUBDIVISION PLAN

- PROPOSED LINE OF SUBDIVISION
- PROPOSED BUILDING FOOTPRINT
- SITE AREA CALCULATION

LEGEND - GFA & CALCULATIONS

- GROSS FLOOR AREA (GFA)
- LANDSCAPING AREA (MIN. 1.5x1.5m)
- PRIVATE OPEN SPACE (MIN. 4x4m)
- ARTICULATION ZONE (1.5m)
- ARTICULATION ELEMENTS (25%)

GENERAL LEGEND

- EXISTING FINISHED FLOOR LEVEL MARKER
- PROPOSED FINISHED FLOOR LEVEL MARKER
- EXISTING FINISHED LEVEL ELEVATION MARKER
- PROPOSED FINISHED LEVEL ELEVATION MARKER
- FLOOR WASTE PENETRATION
- SMOKE ALARM TO AS3786
- DIRECTION AND ANGLE OF INCLINING GRADIENT
- REVIEW / REVISION CLOUD
- PENETRATION ABOVE
- FLOOR PENETRATION BELOW

HYDRAULIC / STORMWATER LEGEND

- DOWNPIPE - REFER TO CIVIL ENGINEERS DETAILS
- PLANTER DRAIN OUTLET
- SPOOD DRAIN OUTLET
- RAIN WATER OUTLET
- STORMWATER PIT - REFER TO CIVIL ENGINEERS DETAILS
- RAIN WATER TANK TO BASIX REQUIREMENTS AND STORMWATER ENGINEERS DETAILS

LEGEND - CONCRETE SETOUT

- INTERNAL FINISHED SLAB LEVEL
- 50MM SETDOWN TO WET AREA
- 100MM SETDOWN TO EXTERNAL

LEGEND - REFLECTED CEILING PLAN

- MOISTURE RESISTANT BOARD - PAINT FINISH
- PLASTER BOARD CEILING - PAINT FINISH
- PLASTER BOARD CEILING - PAINT FINISH
- CEILING/ SOFFIT HEIGHT FROM FFL
- RECESS FOR CURTAIN/BLIND

LEGEND - DEMOLITION PLAN

- EXISTING STRUCTURES TO BE DEMOLISHED. REPAIR & REINSTATE ADJOINING SURFACES.
- EXISTING SITE TO BE REMOVED / DEMOLISHED
- EXISTING TREES TO REMAIN. REFER ALSO TO LANDSCAPE DRAWING.
- EXISTING TREES TO BE REMOVED. REFER ALSO TO LANDSCAPE DRAWING.

-PERFORM ALL THE DEMOLITION AS SHOWN ON THE DRAWING AND/OR AS NECESSARY REQUIRED CARRYING OUT THE WORKS UNDER THE CONTRACT.

-NB: CARE MUST BE TAKEN WHILE CARRING OUT THE WORKS.

-PROTECT EXISTING PROPERTY FROM DAMAGE BY APPROPRIATE MEANS INCLUDING SHORING, STRUTTING, PROTECTIVE SCREENS, SHEETING AND THE LIKE.

-REPAIR & REINSTATE ANY SUCH DAMAGE TO MATCH EXISTING.

-EXISTING SERVICES: DEAL AS APPROPRIATE WITH EXISTING SERVICES INCLUDED IN OR ENCOUNTERED DURING THE COURSE OF THE DEMOLITIONS.


-BEFORE DEMOLISHING AND REMOVING PARTS OF BUILDING HAVING ELECTRICAL WIRING, GAS, SEWER AND WATER PIPES, CONDUIT OR SIMILAR ITEMS EMBEDDED IN THEM, NOTIFY THE PROJECT MANAGER/ SUPERINTENDENT, AUTHORITIES HAVING JURISDICTION, AND MAKE SURE THAT THESE ITEMS ARE OUT OF SERVICE SO THAT THEY CAN BE REMOVED WITHOUT DANGER.

NOTES


- COMMON WALL FIRE SEPARATION CLAUSE 9.3.1 OF THE HOUSING PROVISIONS 2022 (FRL 60/60/60)
- COMMON WALL SOUND SEPARATION CLAUSE 10.7.1 OF THE HOUSING PROVISIONS 2022
- MECHANICAL VENTILATION CLAUSE 10.6.2 OF THE HOUSING PROVISIONS 2022
- SMOKE ALARMS CLAUSE 9.5.4 OF THE HOUSING PROVISIONS 2022
- BALUSTRADES INSTALLATION CLAUSE 11.3.4 OF THE HOUSING PROVISIONS 2022
- PROTECTION OF OPERABLE WINDOWS CLAUSE 11.3.7 OF THE HOUSING PROVISIONS 2022

LEGEND - WALL TYPES


- 250mm BRICK VENEER WALL
- 110mm FACE BRICK + 50mm CAVITY + 90mm TIMBER STUD + 10mm GYPROCK
- 230mm BRICK VENEER WALL
- 110mm FACE BRICK + 10mm CAVITY + 110mm FACE BRICK
- 90mm STUD WALL
- 10mm GYPROCK + 90mm TIMBER STUD + 10mm GYPROCK
- CSR 360 TIMBER FRAMED PARTY WALL SYSTEM
- 10mm GYPROCK + 90mm TIMBER STUD + 20mm CAVITY + 25mm GYPROCK SHAFT LINER PANEL + 90mm TIMBER STUD + 10mm GYPROCK
- 225mm HERAL VENEER WALL
- 10mm ACRYLIC RENDER + 100mm NRG
- Greenboard + 25mm CAVITY + 90mm TIMBER STUD + 10mm GYPROCK

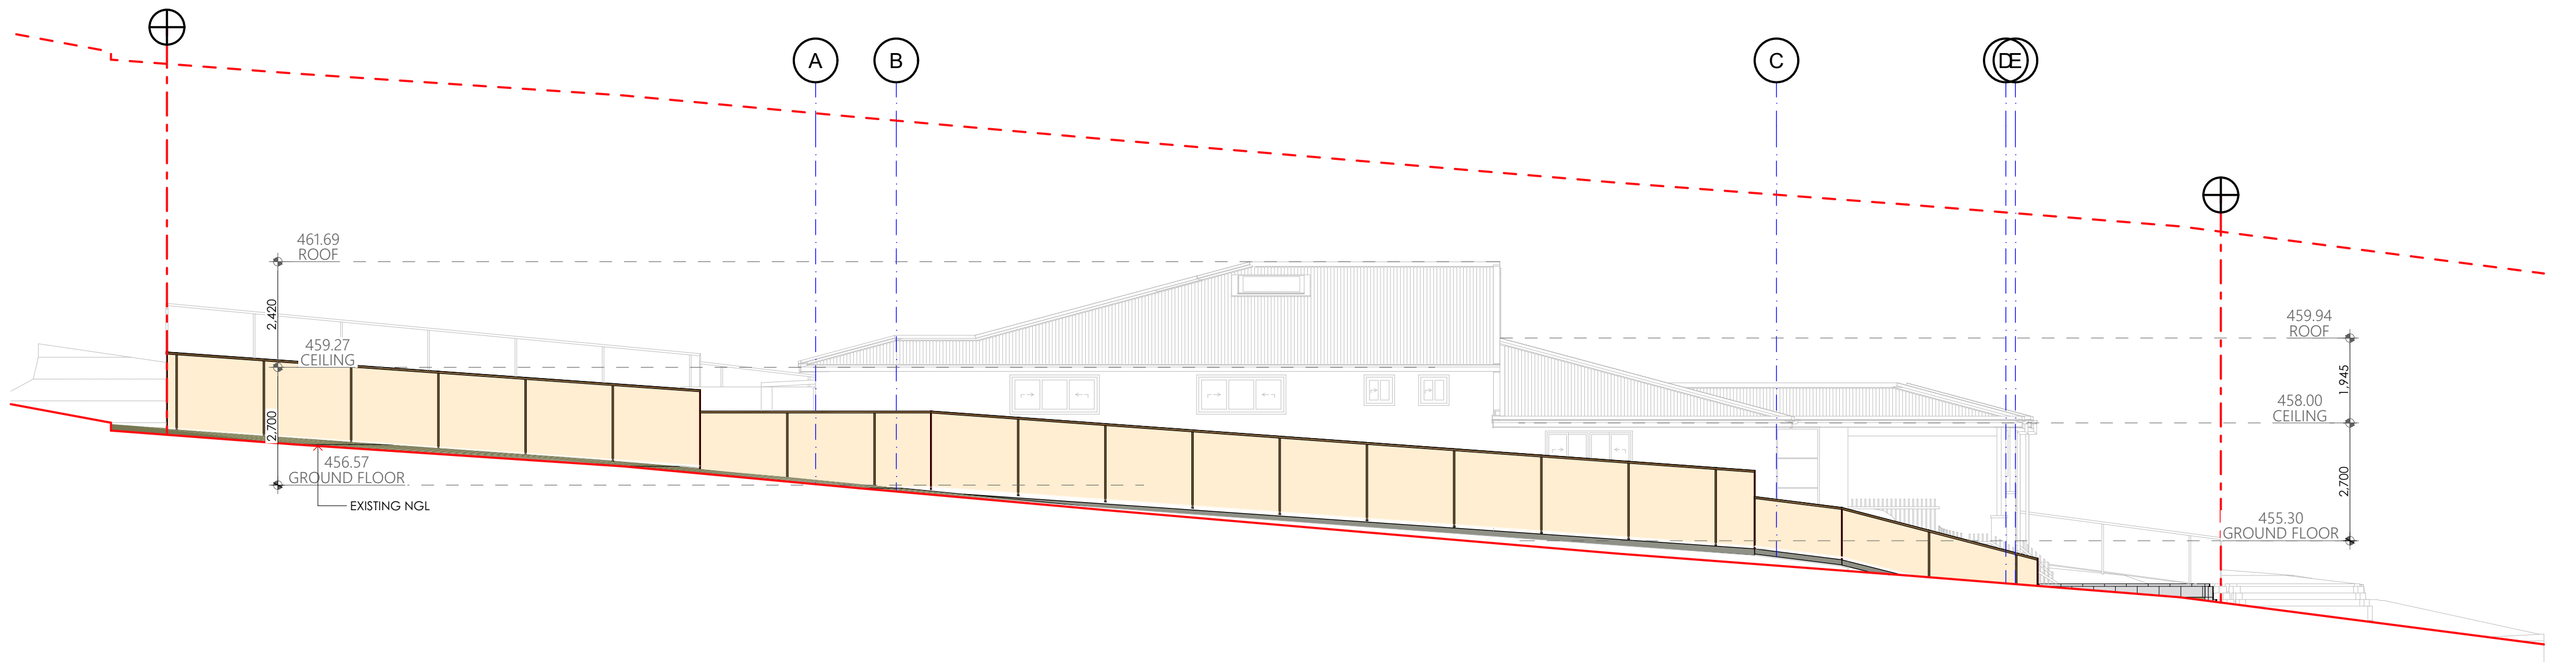


SOUTH EASTERN FENCE ELEVATION
1:100

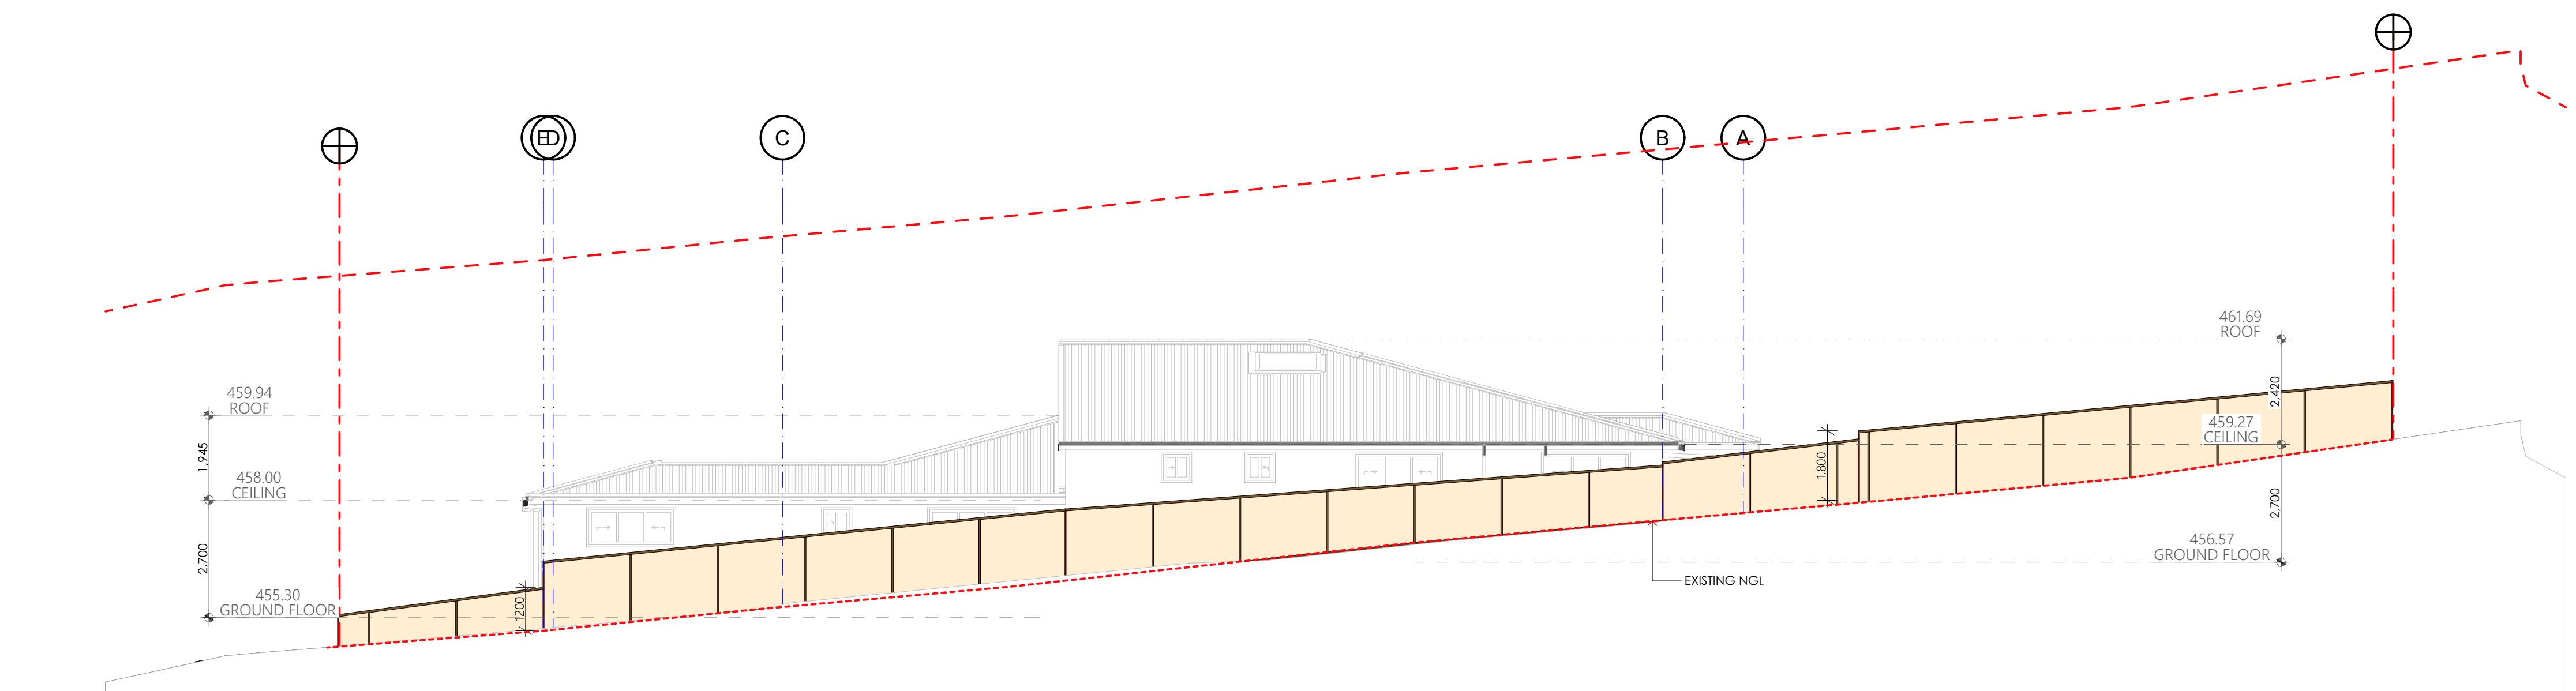

NORTH WESTERN FENCE ELEVATION
1:100

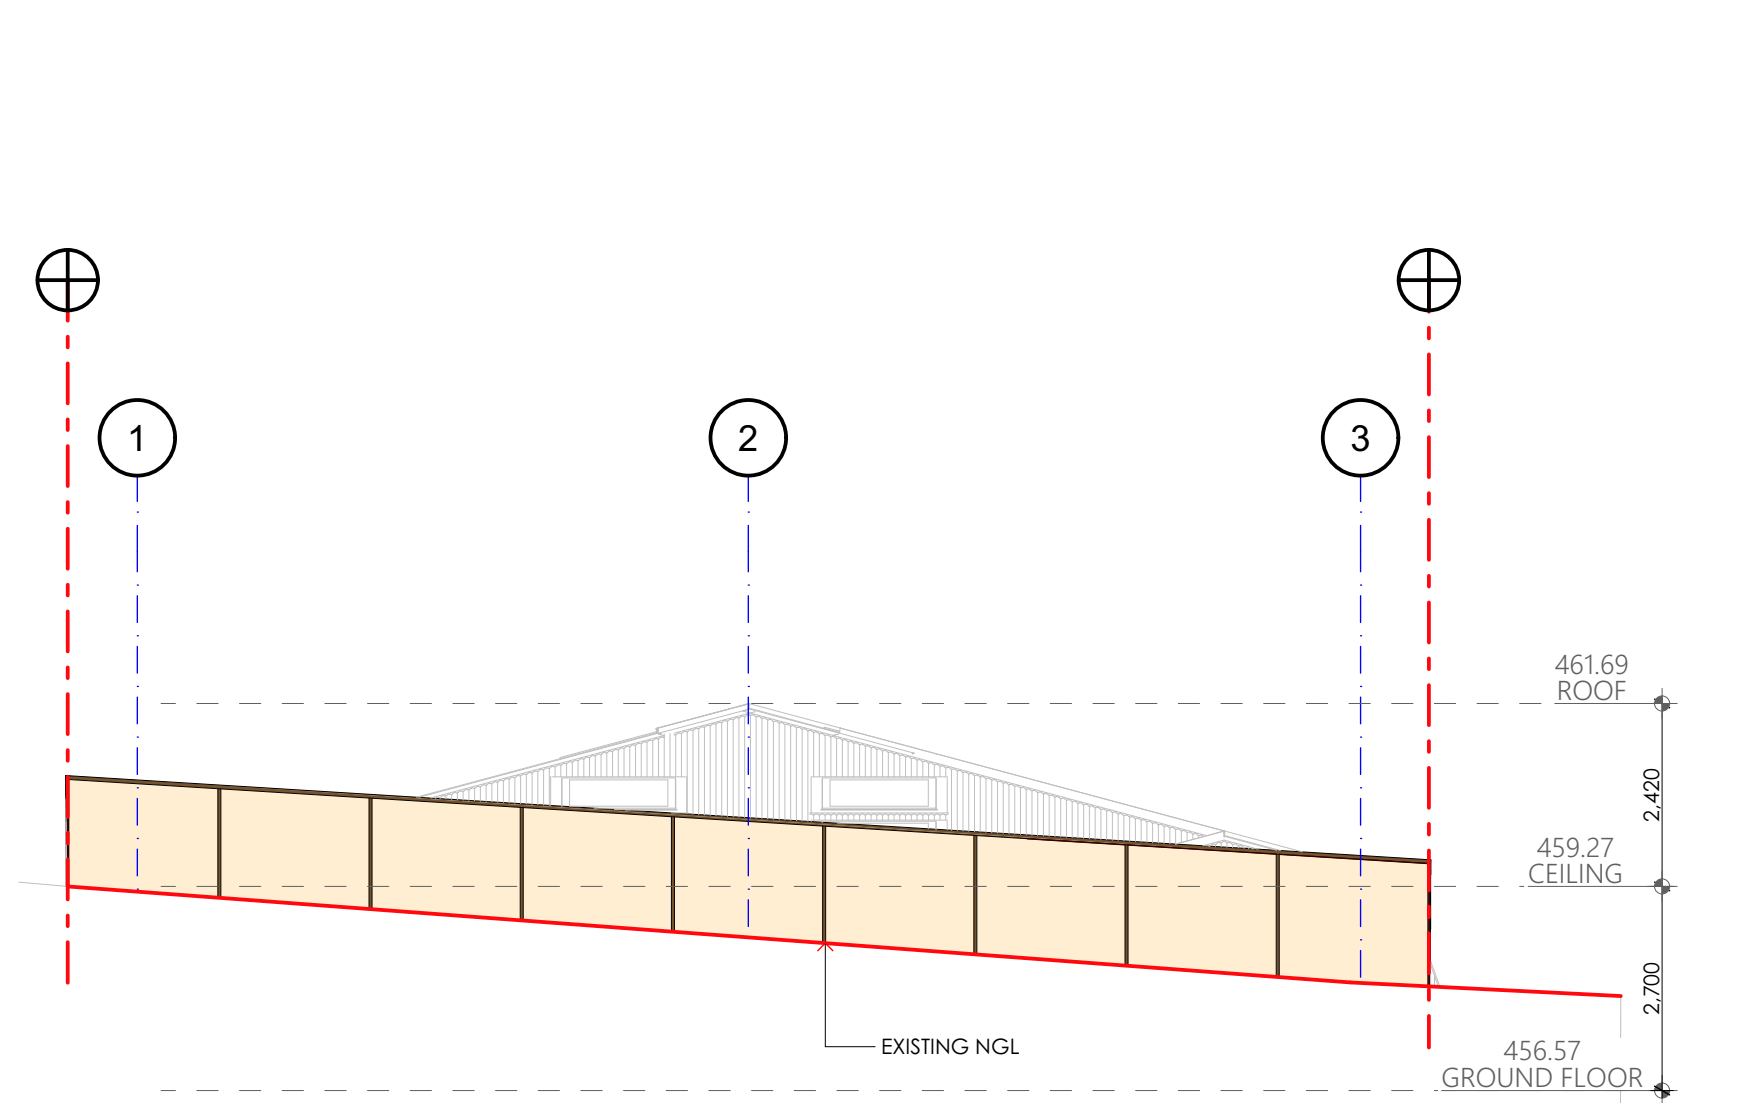


SOUTH WESTERN FENCE ELEVATION
1:100

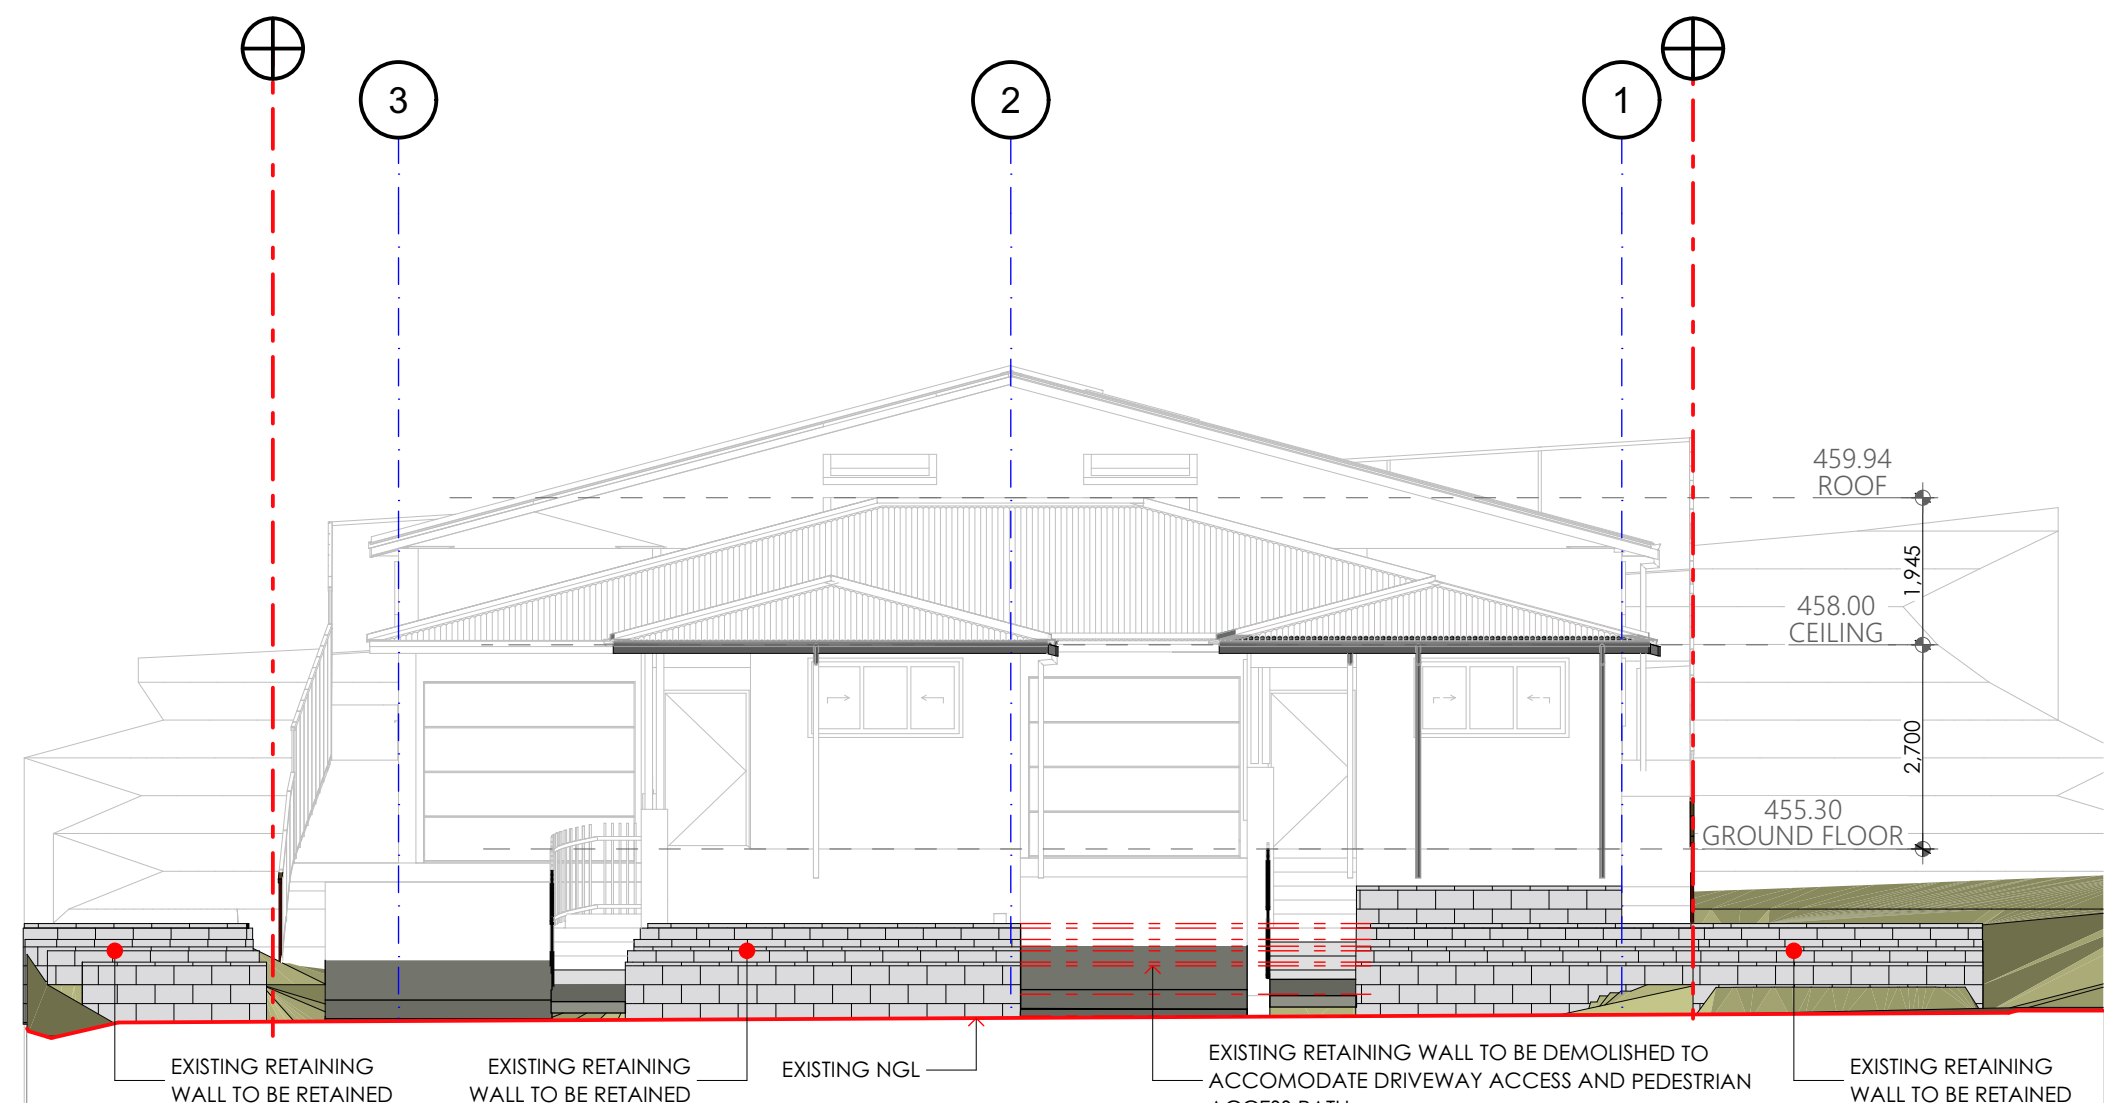

NORTH EASTERN FENCE ELEVATION
1:100

SCHEDULE OF
EXTERNAL MATERIAL &
FINISHES:

PT-1: CEMENT RENDER - PAINT
FINISH - DULUX LEXICON
QUARTER OR SIMILIAR

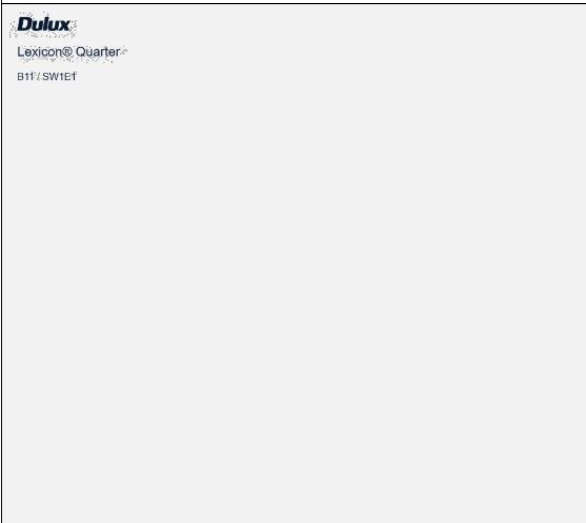

EXTERNAL WINDOW FRAMES
PAINTED DULUX MONUMENT
GREY




FB-1: PGH MORADA CENIZA
OR SIMILIAR



ST-1:
STONE FEATURE WALL
QUARTER OR SIMILIAR




COLOURBOND PALE
EUCALYPT FENCE

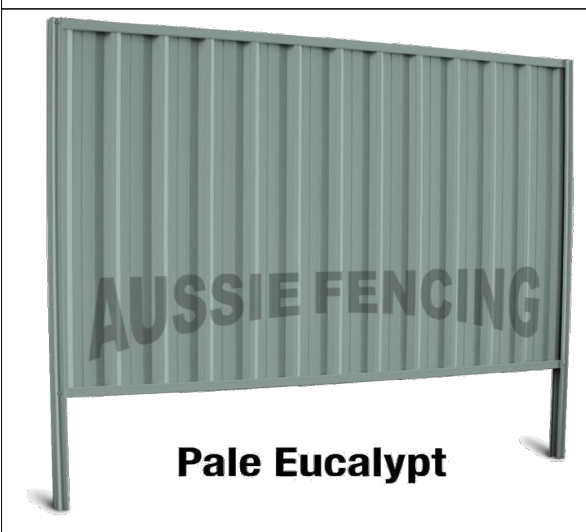

ISSUE	DESCRIPTION	DATE
03	ISSUED FOR DA APPROVAL	8/08/2025
04	ISSUED FOR DA APPROVAL	22/10/2025
05	ISSUED FOR DA APPROVAL	7/11/2025
06	ISSUED FOR C.C. COORDINATION	2/03/2026
07	ISSUED FOR C.C. APPROVAL	4/05/2026

NOTES
The plans, drawings and specifications incorporated in this document shall remain the copyright © of ECOTECH DESIGNS PTY LTD and must not be used, reproduced or copied wholly or in part without prior written consent of ECOTECH DESIGNS PTY LTD.
Figured dimensions shall take preference over scaling. Verify all dimensions on site.

SCALE
1:100 @ A1 or 1:200 @ A3


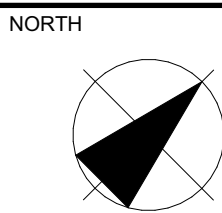


DRAWING TITLE
FENCE ELEVATIONS
DRAWING NO
CC10







PROPOSED ATTACHED DUAL OCCUPANCY
26 MARSKELL CIRCUIT MUDGEE

JOB NO. 25008	DATE 4/05/2026	DRAWN P.G	CHECKED P.G	SCALE As Shown on A1
------------------	-------------------	--------------	----------------	-------------------------






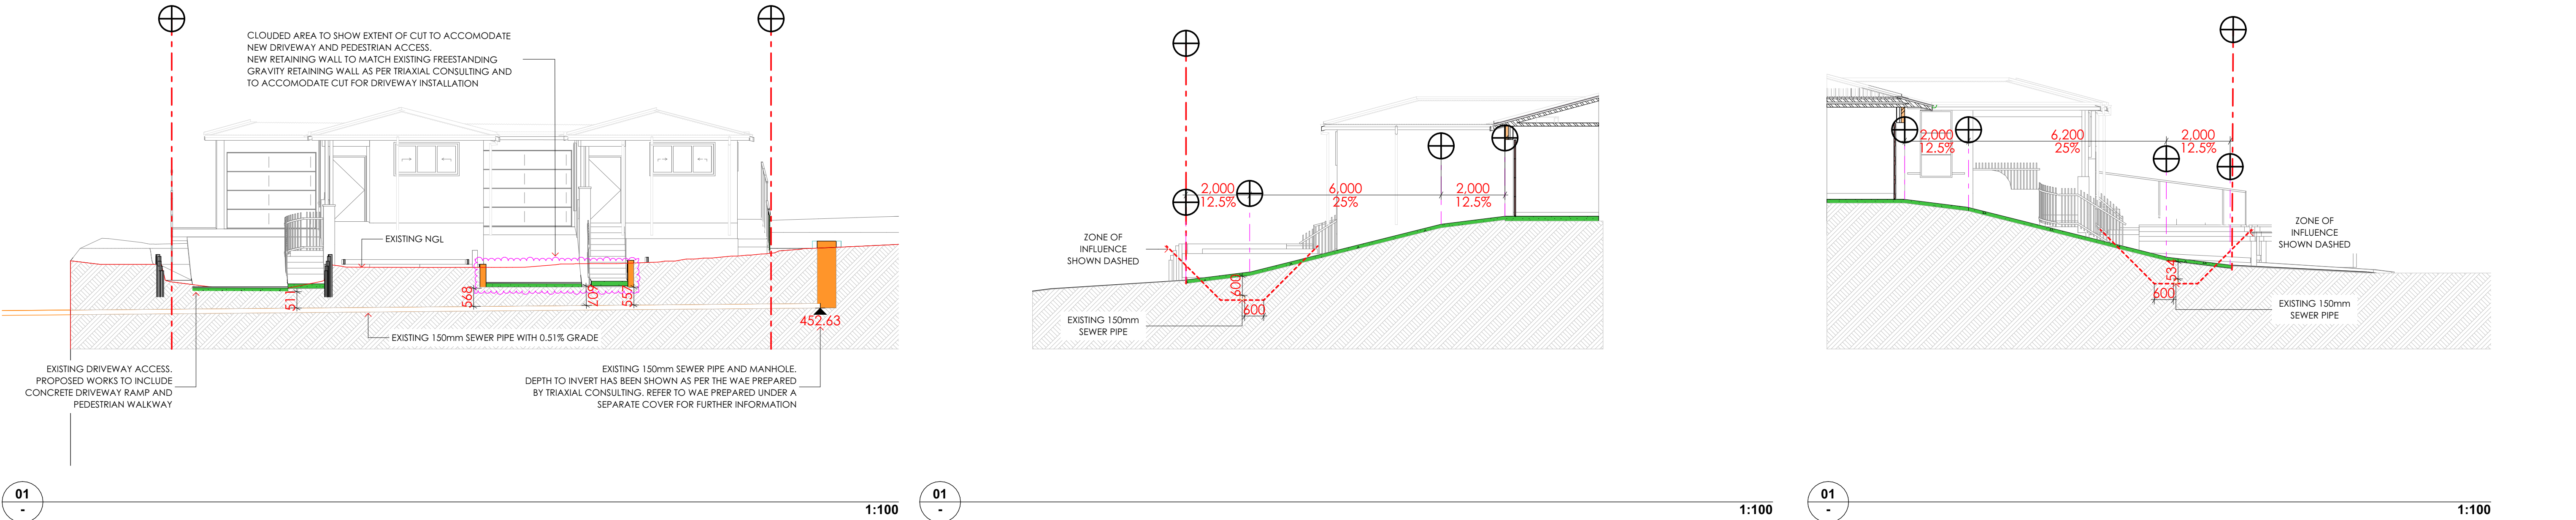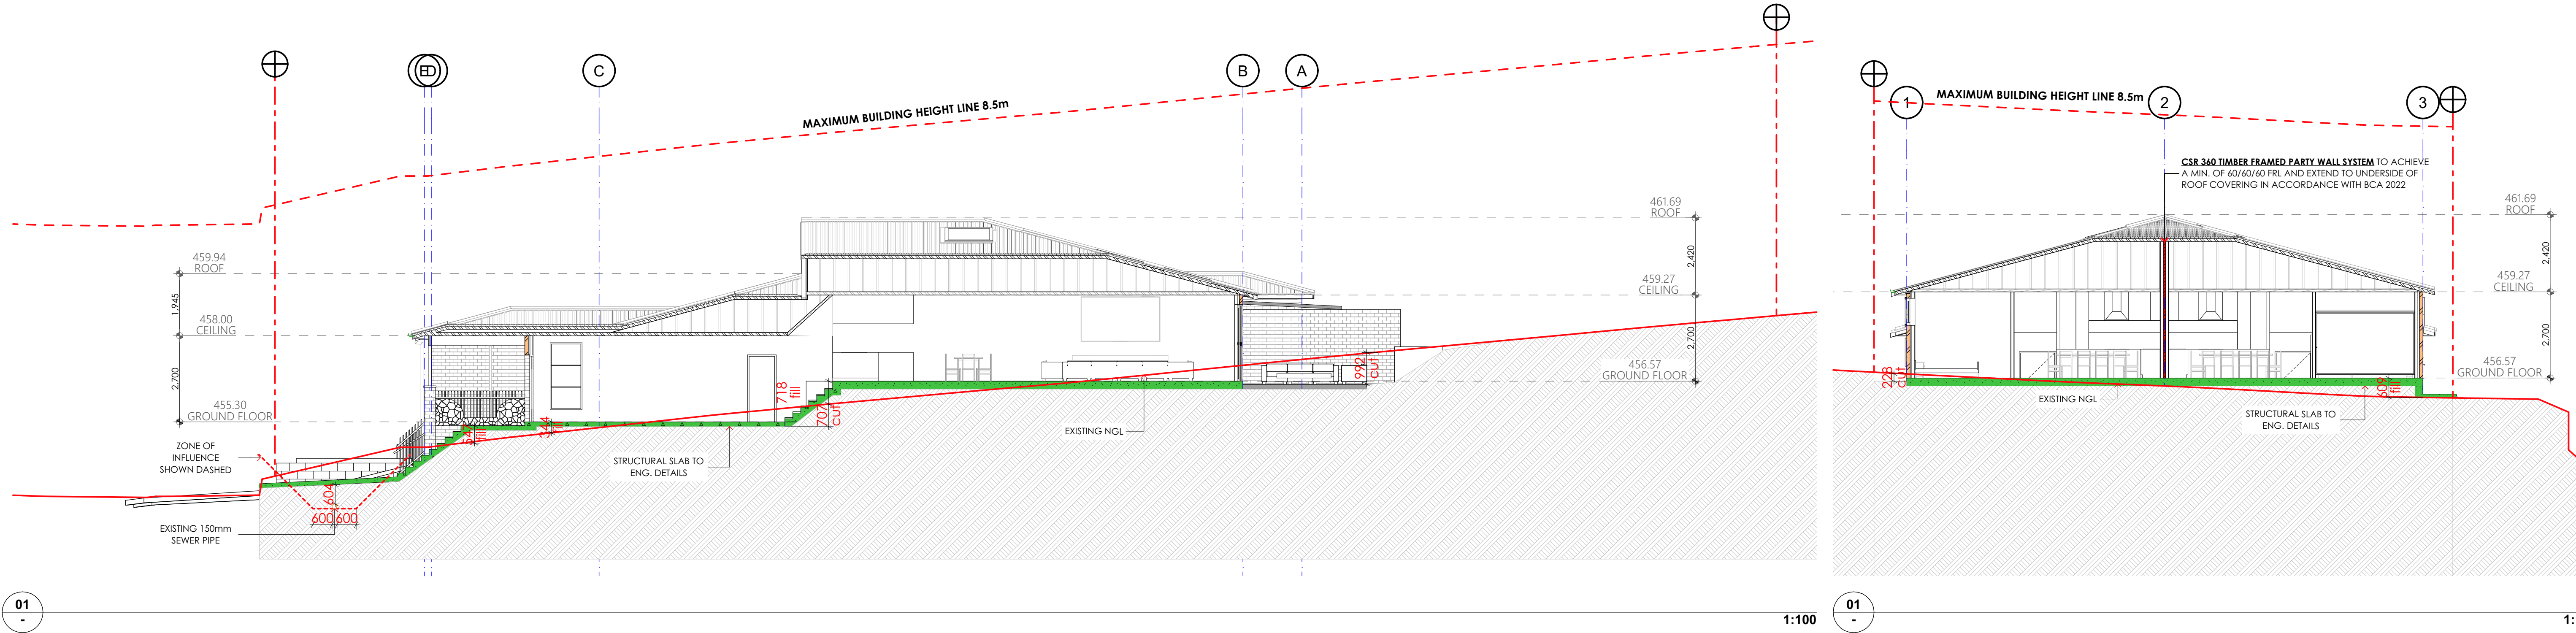

ISSUE	DESCRIPTION	DATE	NOTES	SCALE	NORTH	DRAWING TITLE	PROPOSED ATTACHED DUAL OCCUPANCY 26 MARSKELL CIRCUIT MUDGEE					 ECOTECH DESIGNS BUILDING DREAMS SUSTAINABLY
01	ISSUED FOR DA APPROVAL	9/05/2025	The plans, drawings and specifications incorporated in this document shall remain the copyright © of ECOTECH DESIGNS PTY LTD and must not be used, reproduced or copied wholly or in part without prior written consent of ECOTECH DESIGNS PTY LTD. Figured dimensions shall take preference over scaling. Verify all dimensions on site.	1:100 @ A1 or 1:200 @ A3		SECTIONS DRAWING NO CC11						
03	ISSUED FOR DA APPROVAL	8/08/2025										
04	ISSUED FOR DA APPROVAL	22/10/2025										
05	ISSUED FOR DA APPROVAL	7/11/2025										
06	ISSUED FOR CC COORDINATION	2/03/2026										
07	ISSUED FOR CC APPROVAL	4/05/2026										
							JOB NO. 25008	DATE 4/05/2026	DRAWN P.G	CHECKED P.G	SCALE As Shown on A1	

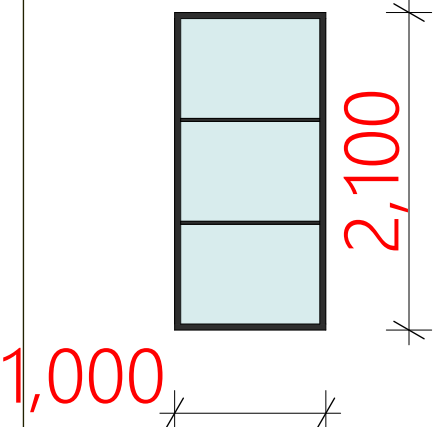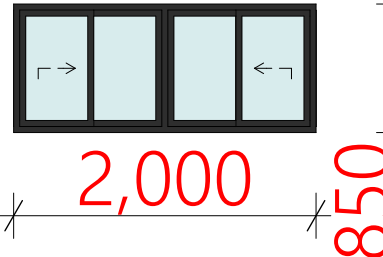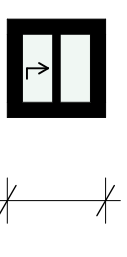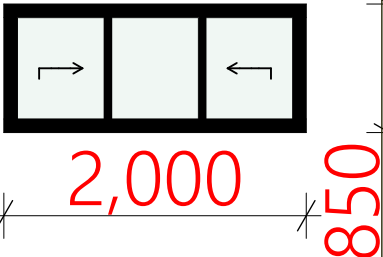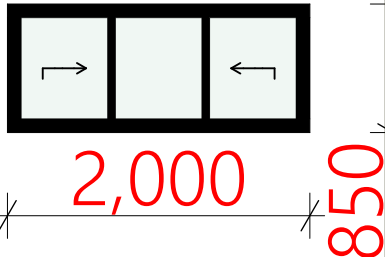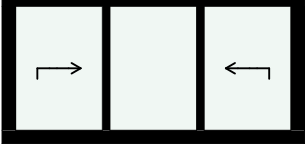Window List						
Window ID	W01	W02	W03	W04	W05	W06
W x H Size	1,000×2,100	2,000×850	650×650	2,000×850	2,000×850	2,000×1,000
Window sill hei...	500	1,850	1,850	1,650	1,350	1,500
Elevational View						
Quantity	2	1	5	6	1	2

1	Window List
-	

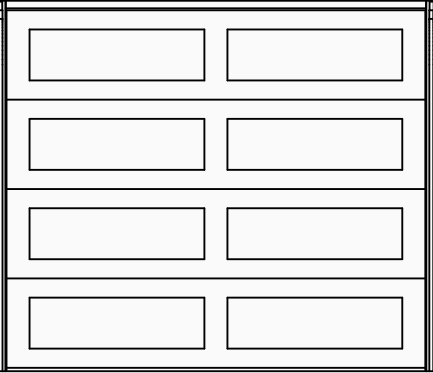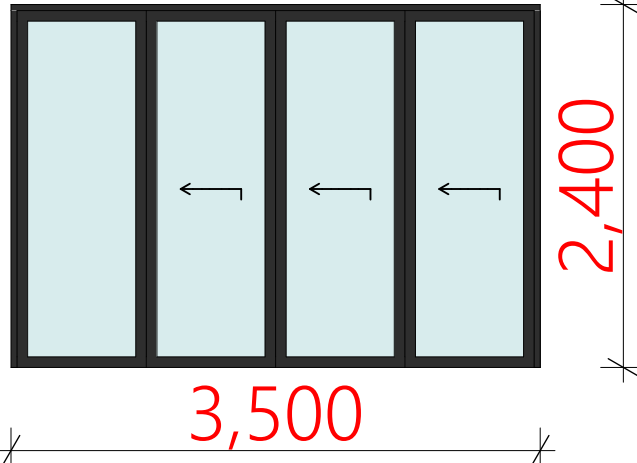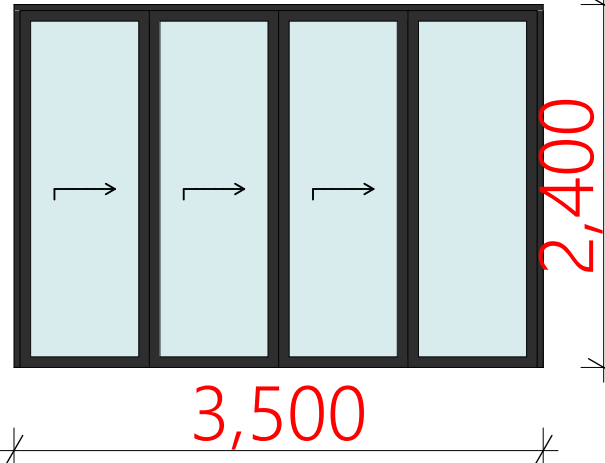Door List			
Door Name	Overhead Garage Door 27	Sliding Door 27	Sliding Door 27
Quantity	2	1	1
W x H Size	2,800×2,400	3,500×2,400	3,500×2,400
Door head height	2,400	300	2,400
3D Front View			

2	Door List
-	

BCA NOTES
Refer to Parts 8.3, 8.4, 11.3.7, 11.3.8 of The BCA and NOTES Below;


Glass - Application
Glazing must comply with the following:
(a) 8.3.2 for glass sizes and installation.
(b) 8.3.3 for fully framed glazing installed in the perimeter of buildings.
(c) Part 8.4 for glazed assemblies subject to human impact.
(d) Glass used must be of a type within the scope of AS 1288.
(e) Glass used in barriers, except a window serving as a barrier, must withstand loading forces in accordance with AS 1170.1.
(f) Safety glass must be—
(i) legibly marked in accordance with 8.4.7; and
(ii) made visible in accordance with 8.4.8.

Glazing Human Impact - Application
(1) Part 8.4 applies subject to the limitations set out in H1D8(1).
(2) Part 8.4 need not be complied with if H1D8(3) is complied with.
(3) The thickness and type of glazing installed in areas of a building that have a high potential for human impact (an area of a building frequented by the occupants during everyday activities in which a person could fall into or against the glazed panel) must comply as follows:
(a) Doors — in accordance with 8.4.2.
(b) Door side panels — in accordance with 8.4.3.
(c) Full height glass panels — in accordance with 8.4.4.
(d) Glazed panels, other than doors or side panels, on the perimeter of rooms — in accordance with 8.4.5.
(e) Bathrooms, ensuite and spa room glazing — in accordance with 8.4.6.
(f) Visibility of glazing — in accordance with 8.4.7.
(g) Identification of safety glass — in accordance with 8.4.8.

Protection of openable windows - Bedrooms
(1) A window opening in a bedroom must be provided with protection, where the floor below the window is 2 m or more above the surface beneath.
(2) Where the lowest level of the window opening covered by (1) is less than 1.7 m above the floor, the window opening must comply with the following:
(a) The openable portion of the window must be protected with—
(i) a device capable of restricting the window opening; or
(ii) a screen with secure fittings.
(b) A device or screen required by (a) must—
(i) not permit a 125 mm sphere to pass through the window opening or screen; and
(ii) resist an outward horizontal action of 250 N against the—
(A) window restrained by a device; or
(B) screen protecting the opening; and
(iii) have a child resistant release mechanism if the screen or device is able to be removed, unlocked or overridden.
(3) Where a device or screen provided in accordance with (2)(a) is able to be removed, unlocked or overridden, a barrier with a height not less than 865 mm above the floor is required to an openable window in addition to window protection.
(4) A barrier covered by (3) must not—
(a) permit a 125 mm sphere to pass through it; and
(b) have any horizontal or near horizontal elements between 150 mm and 760 mm above the floor that facilitate climbing (see Figure 11.3.7).
(1) A window opening in a room other than a bedroom must be provided with protection where the floor below the window is 4 m or more above the surface beneath.
(2) The openable part of the window covered by (1) must be protected with a barrier with a height of not less than 865mm above the floor.
(3) A barrier required by (2) must not—
(a) permit a 125 mm sphere to pass through it; and
(b) have any horizontal or near horizontal elements between 150 mm and 760 mm above the floor that facilitate climbing.

LEGEND	
	PROPOSED GFA
	POS
	LANDSCAPE AREA
	ARTICULATION

DEVELOPMENT DATA	
SITE AREA: 854.8m2	
MAX. ALLOWABLE GFA = 427.4m2	
PROPOSED GFA = 385.70	
PROPOSED LANDSCAPE = 270.48	

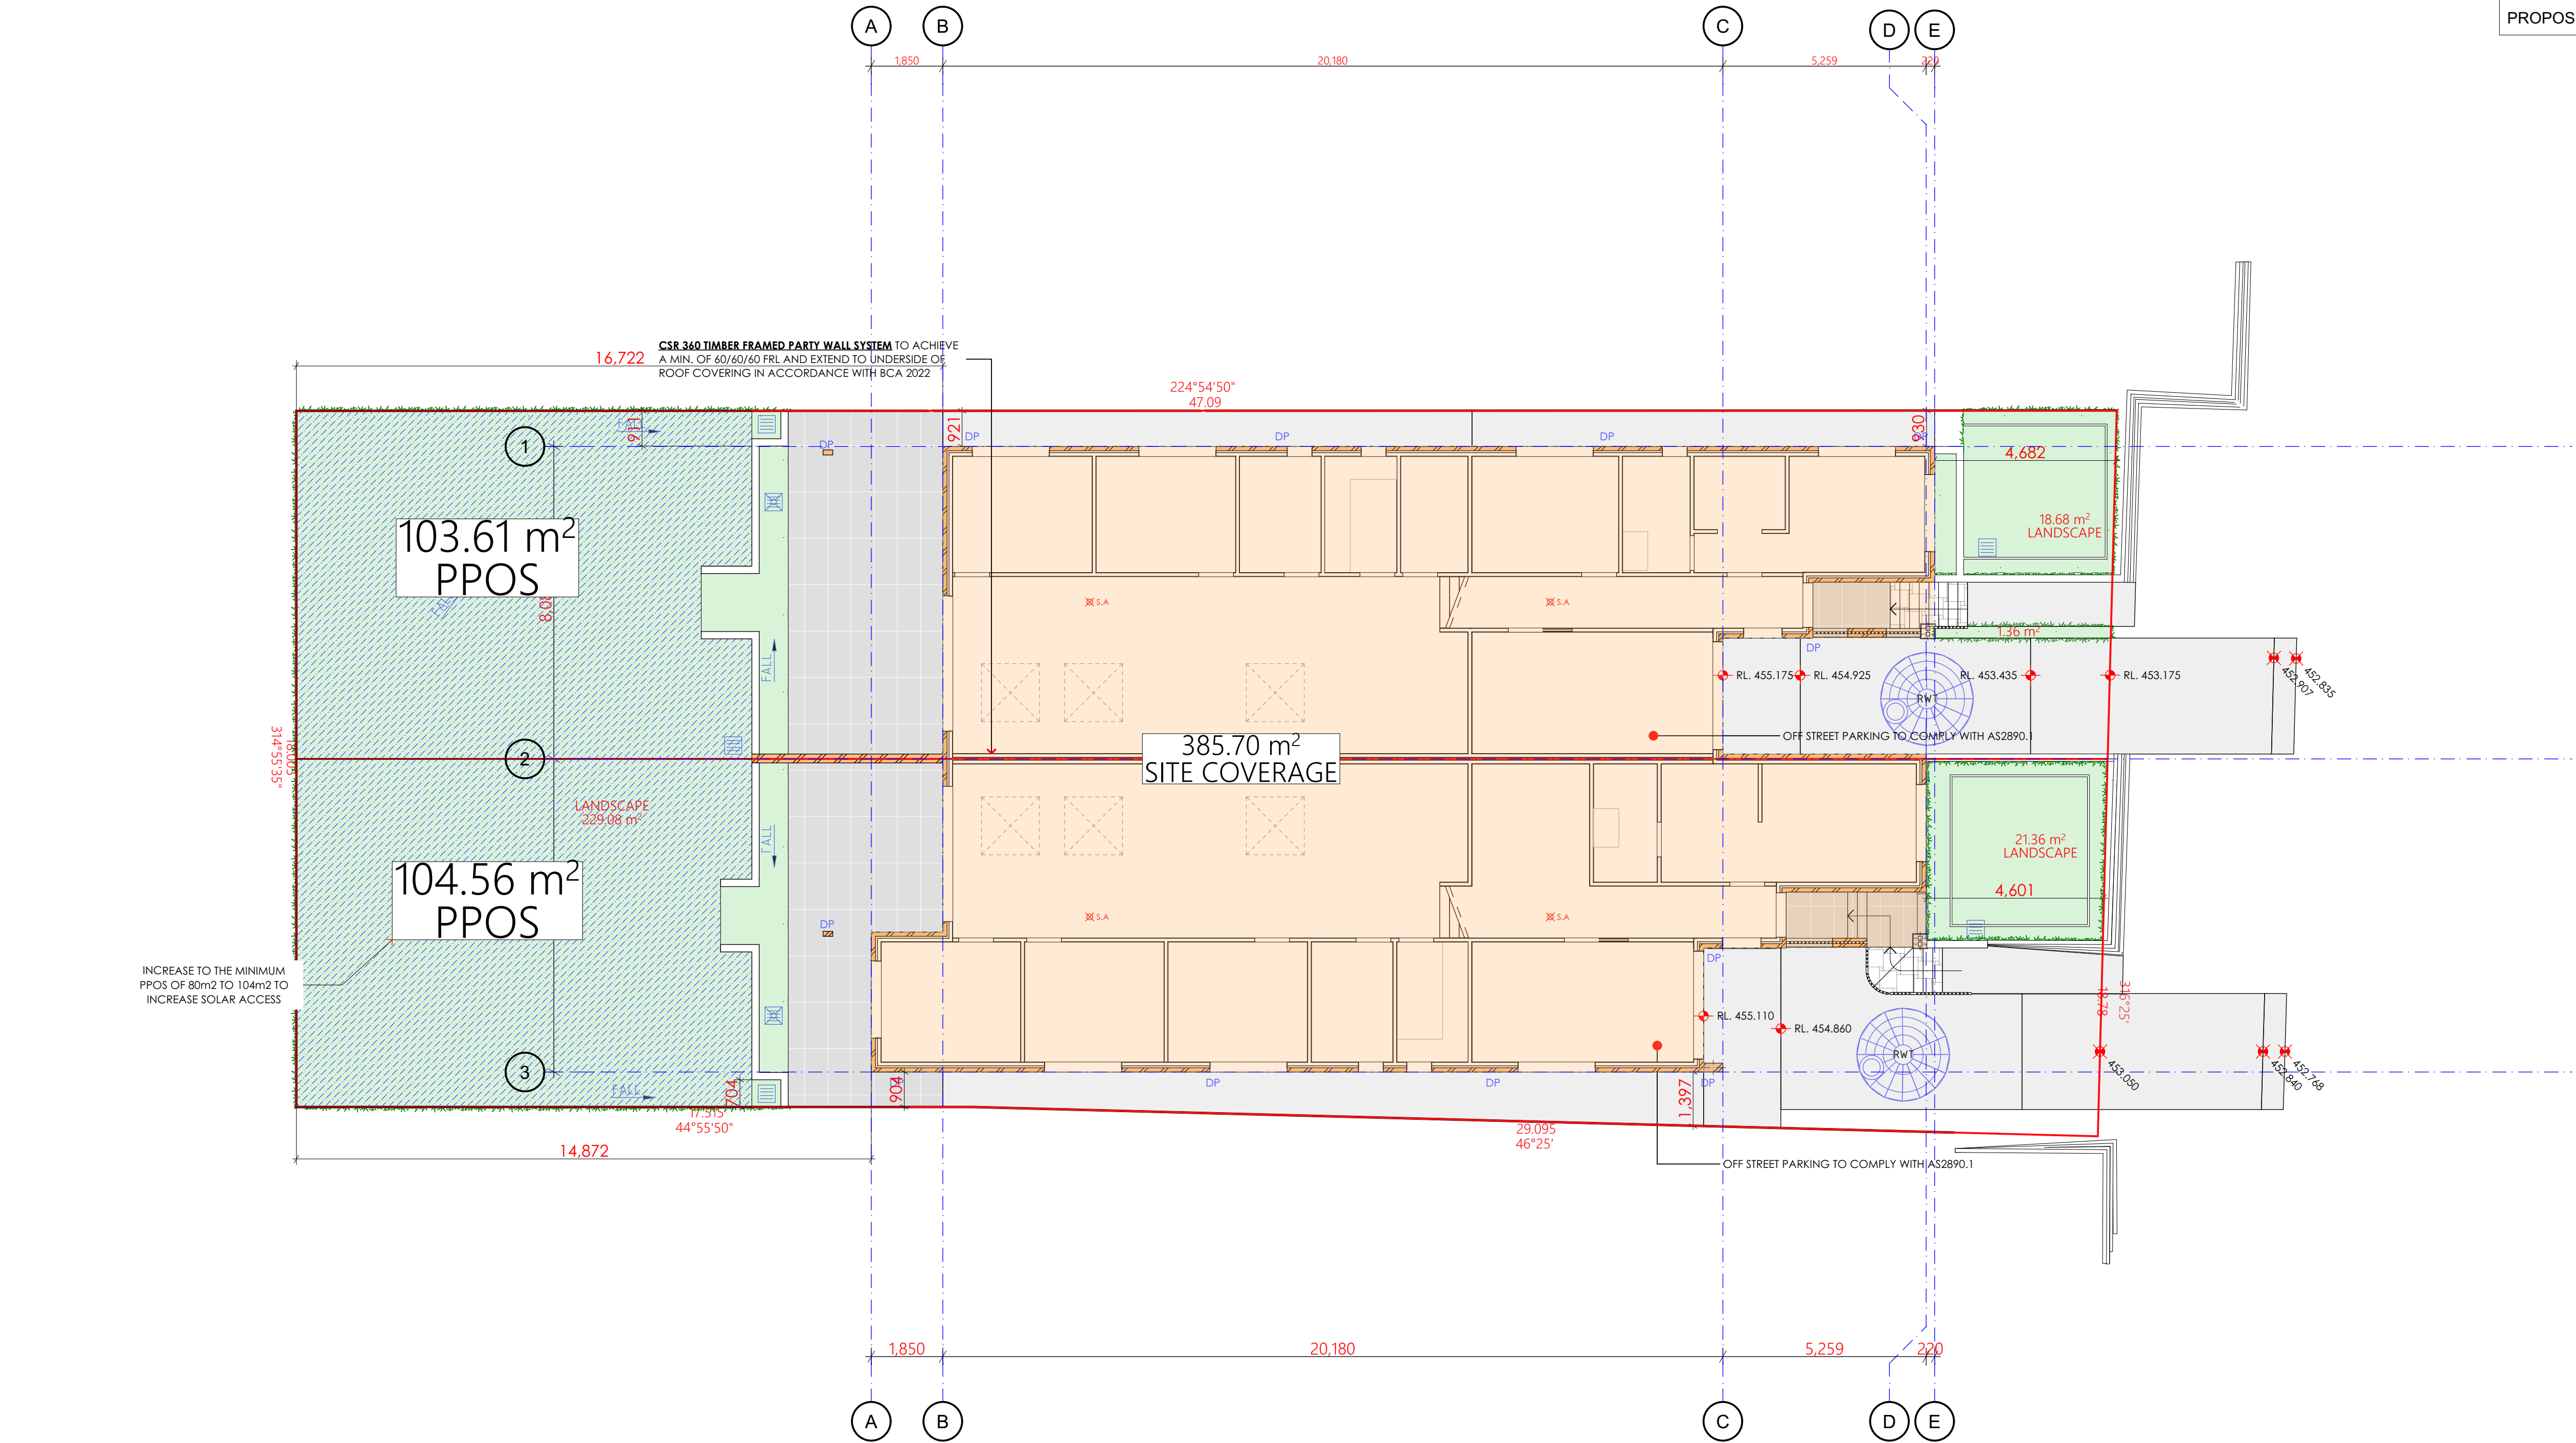

01

GROUND FLOOR CALCULATION PLAN
1:100

ISSUE	DESCRIPTION	DATE	NOTES	SCALE	NORTH	DRAWING TITLE	PROPOSED ATTACHED DUAL OCCUPANCY 26 MARSKELL CIRCUIT MUDGEE					 ECOTECH DESIGNS BUILDING DREAMS SUSTAINABLY		
01	ISSUED FOR DA APPROVAL	9/05/2025	The plans, drawings and specifications incorporated in this document shall remain the copyright © of ECOTECH DESIGNS PTY LTD and must not be used, reproduced or copied wholly or in part without prior written consent of ECOTECH DESIGNS PTY LTD. Figured dimensions shall take preference over scaling. Verify all dimensions on site.	1:100 @ A1 or 1:200 @ A3		CALCULATION PLANS DRAWING NO CC13								
03	ISSUED FOR DA APPROVAL	8/08/2025												
04	ISSUED FOR DA APPROVAL	22/10/2025												
05	ISSUED FOR DA APPROVAL	7/11/2025												
06	ISSUED FOR CC COORDINATRION	2/03/2026												
07	ISSUED FOR CC APPROVAL	4/05/2026												
							JOB NO. 25008	DATE 4/05/2026	DRAWN P.G	CHECKED P.G	SCALE As Shown on A1			

SCHEDULE OF EXTERNAL MATERIAL & FINISHES:

ST-1:
STONE FEATURE WALL
QUARTER OR SIMILIAR



PT-1:
CEMENT RENDER -
PAINT FINISH - DULUX
LEXICON QUARTER OR
SIMILIAR



FB-1:
PGH MORADA CENIZA
OR SIMILIAR



EXTERNAL WINDOW
FRAMES PAINTED
DULUX MONUMENT
GREY



COLOURBOND PALE
EUCALYPT FENCE

