

DEVELOPMENT SUMMARY

	REQUIREMENT	PROPOSED	COMPLIANCE
MIN. LOT SIZE	400m²	708.20 m²	Y
ZONE	-	R2	Y
BUILDING HEIGHT	MAX. 8.5 m	7.3 m	Y
GFA	477.05 m²	421.3m²	Y
25% of SITE AREA + 300 m²			
FRONT SETBACK	(7.405m + 9.065m)/2=8.235m	8.235m	Y
SIDE SETBACK			
PARENT LOT WIDTH 12m-24m			Y
building height 0m-4.5m	0.9m	1.120m	
building height >4.5m-8.5m	(7.3-4.5m)/4+0.9m = 1.60	1.605m	
REAR SETBACK			
LOT AREA 400m²-900m²			Y
building height 0m-4.5m	3m	14m	
building height >4.5m-8.5m	8m	14m	
DWELLING CONFIGURATION	- Each dwelling must face a public road - Each dwelling, incl. an off-street car parking space must have a min. width of 6.5m	- Direct access to Johnston Ave available - Building width each 6.5m	Y
BALCONY, DECKS, PATIO, TERRACES & VERANDAH	- Max height of the floor level is 4m. - Any attached side or rear that has a floor level of more than 2m above ground level (existing) must have a setback from side and rear boundaries of at least 3m - Total area must no be more than 12m²	Balcony Height 4m	Y
LANDSCAPING			
(min dimension 1.5m x 1.5m)			
MIN. LANDSCAPE AREA	254.1 m²	255.8m²	Y
(50% of Site area - 100 m²)			
FRONT LANDSCAPE AREA	63.52 m²	65m²	Y
25% of the area forward of the front building line			
REAR LANDSCAPE REAR	127.05 m²	141.4m²	Y
50% of total landscape required			
PRIVATE OPEN SPACE	16m²	16m²	Y
(min dimension 3m)			

NatHERS ASSESSMENT

Climate Zone: 28, Richmond
Lowest Conditioned Floor: Concrete slab on ground

	Star Rating	Energy Usage (MJ/m²)		
		Heating Load	Cooling Load	Total
Limit	7	25	18	-
3A	7.0	14.9	14.9	29.8
3B	7.4	12.4	14.1	26.5

3A Johnston Avenue, Kirrawee			
ROOF and CEILING: Flat metal roof			
- R5.0 bulk ceiling insulation and reflective sisalation under the roof			
FLOORS: Concrete slab on ground, suspended slab first floor			
- No insulation to the concrete slab on ground or suspended first floor			
WALLS: As per plans			
- R1.5 foamboard between the double brick walls, excluding the garage external walls			
- No insulation between the double brick Parti-walls			
- R2.5 insulation to all other external walls with stud walls			
- R2.5 insulation to the internal stud walls of both bathrooms			
GLAZING: Aluminium frame specifications			
Description	Type	Glazing	Specification
WA2, WA3, WA4 & WA7	Sliding windows	Clear single glazing	U-value: 6.16, SHGC: 0.65
All other	Sliding windows	Clear double glazing with argon gap	U-value: 3.73, SHGC: 0.59
All	Fixed	Clear double glazing with argon gap	U-value: 2.98, SHGC: 0.64
All	Sliding doors	Clear double glazing with argon gap	U-value: 3.82, SHGC: 0.61

3B Johnston Avenue, Kirrawee			
ROOF and CEILING: Flat metal roof			
- R5.0 bulk ceiling insulation and reflective sisalation under the roof			
FLOORS: Concrete slab on ground, suspended slab first floor			
- No insulation to the concrete slab on ground or suspended first floor			
WALLS: As per plans			
- R1.5 foamboard between the double brick walls, including the garage external walls			
- No insulation between the double brick Parti-walls			
- R2.5 insulation to all other external walls with stud walls			
- R2.5 insulation to the internal stud walls of both bathrooms			
GLAZING: Aluminium frame specifications			
Description	Type	Glazing	Specification
WB2, WB3, WB4 & WB7	Sliding windows	Clear single glazing	U-value: 6.16, SHGC: 0.65
All other	Sliding windows	Clear double glazing with argon gap	U-value: 3.73, SHGC: 0.59
All	Fixed	Clear double glazing with argon gap	U-value: 2.98, SHGC: 0.64
All	Sliding doors	Clear double glazing with argon gap	U-value: 3.82, SHGC: 0.61

Beyond Certification (Sonder Projects Pty Ltd)
Reference: 3125176CDC
Date: 17/11/2025

Chen Wu
Certifier
BDC3224


BEYOND

COPYRIGHT & GENERAL NOTE:
Figured dimensions shall be taken in preference to scaling. Drawing to be read in conjunction with information on first page. Check all dimensions and levels on site before commencing work or ordering materials. All existing ground lines & levels location are approximate, therefore, to be verified on-site by the builder. Any discrepancies to be verified back to Zhinar Architects before proceeding. All workmanship and materials shall comply with all relevant codes, ordinances, Australian Standards and manufacturers' instructions. Unless noted issued for Constructor drawing not to be used for construction. All art / graphic representations are indicative only. Information on this drawing is the copyright of Zhinar Architects. Copying or using this drawing in whole or part without written permission infringes copyright.

C	ISSUE FOR CDC SUBMISSION 3
B	ISSUE FOR CDC SUBMISSION 2
A	ISSUE FOR CDC SUBMISSION
ISSUE	AMENDMENT

7/11/2025	TH	IC
28/10/2025	TH	IC
18/09/2025	TH	IC
DATE	DRAWN	CHECK


Drawing is NOT VALID or issued for use, unless checked

PROJECT ARCHITECTS
IAN CONRY


Member
Australian
Institute of
Architects

REGISTRATION NUMBER
NSW No. 8317


www.1100.com.au

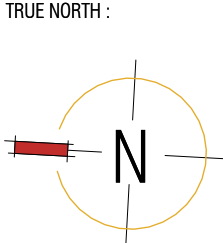

Zhinar Architects Pty Ltd
Suite 1, Level 2
2 Rowe Street
Eastwood, NSW 2122
+61 2 8893 8888 /o
info@zhinar.com.au /e
www.zhinar.com.au /w
28 495 869 790 /abn

PROJECT STATUS :
Complying Development Certificate

PROJECT NAME
Dual Occupancy

3 Johnston Ave

Kirrawee, NSW 2232
L.G.A.: SUTHERLAND SHIRE COUNCIL

SHEET TITLE:
DEVELOPMENT SUMMARY

Checked
Checker


8848
JOB No.

CDC 001
DRAWING No.

C
ISSUE

01234510
scale 1:100 @A1sheet

SCALE @A1 SHEET

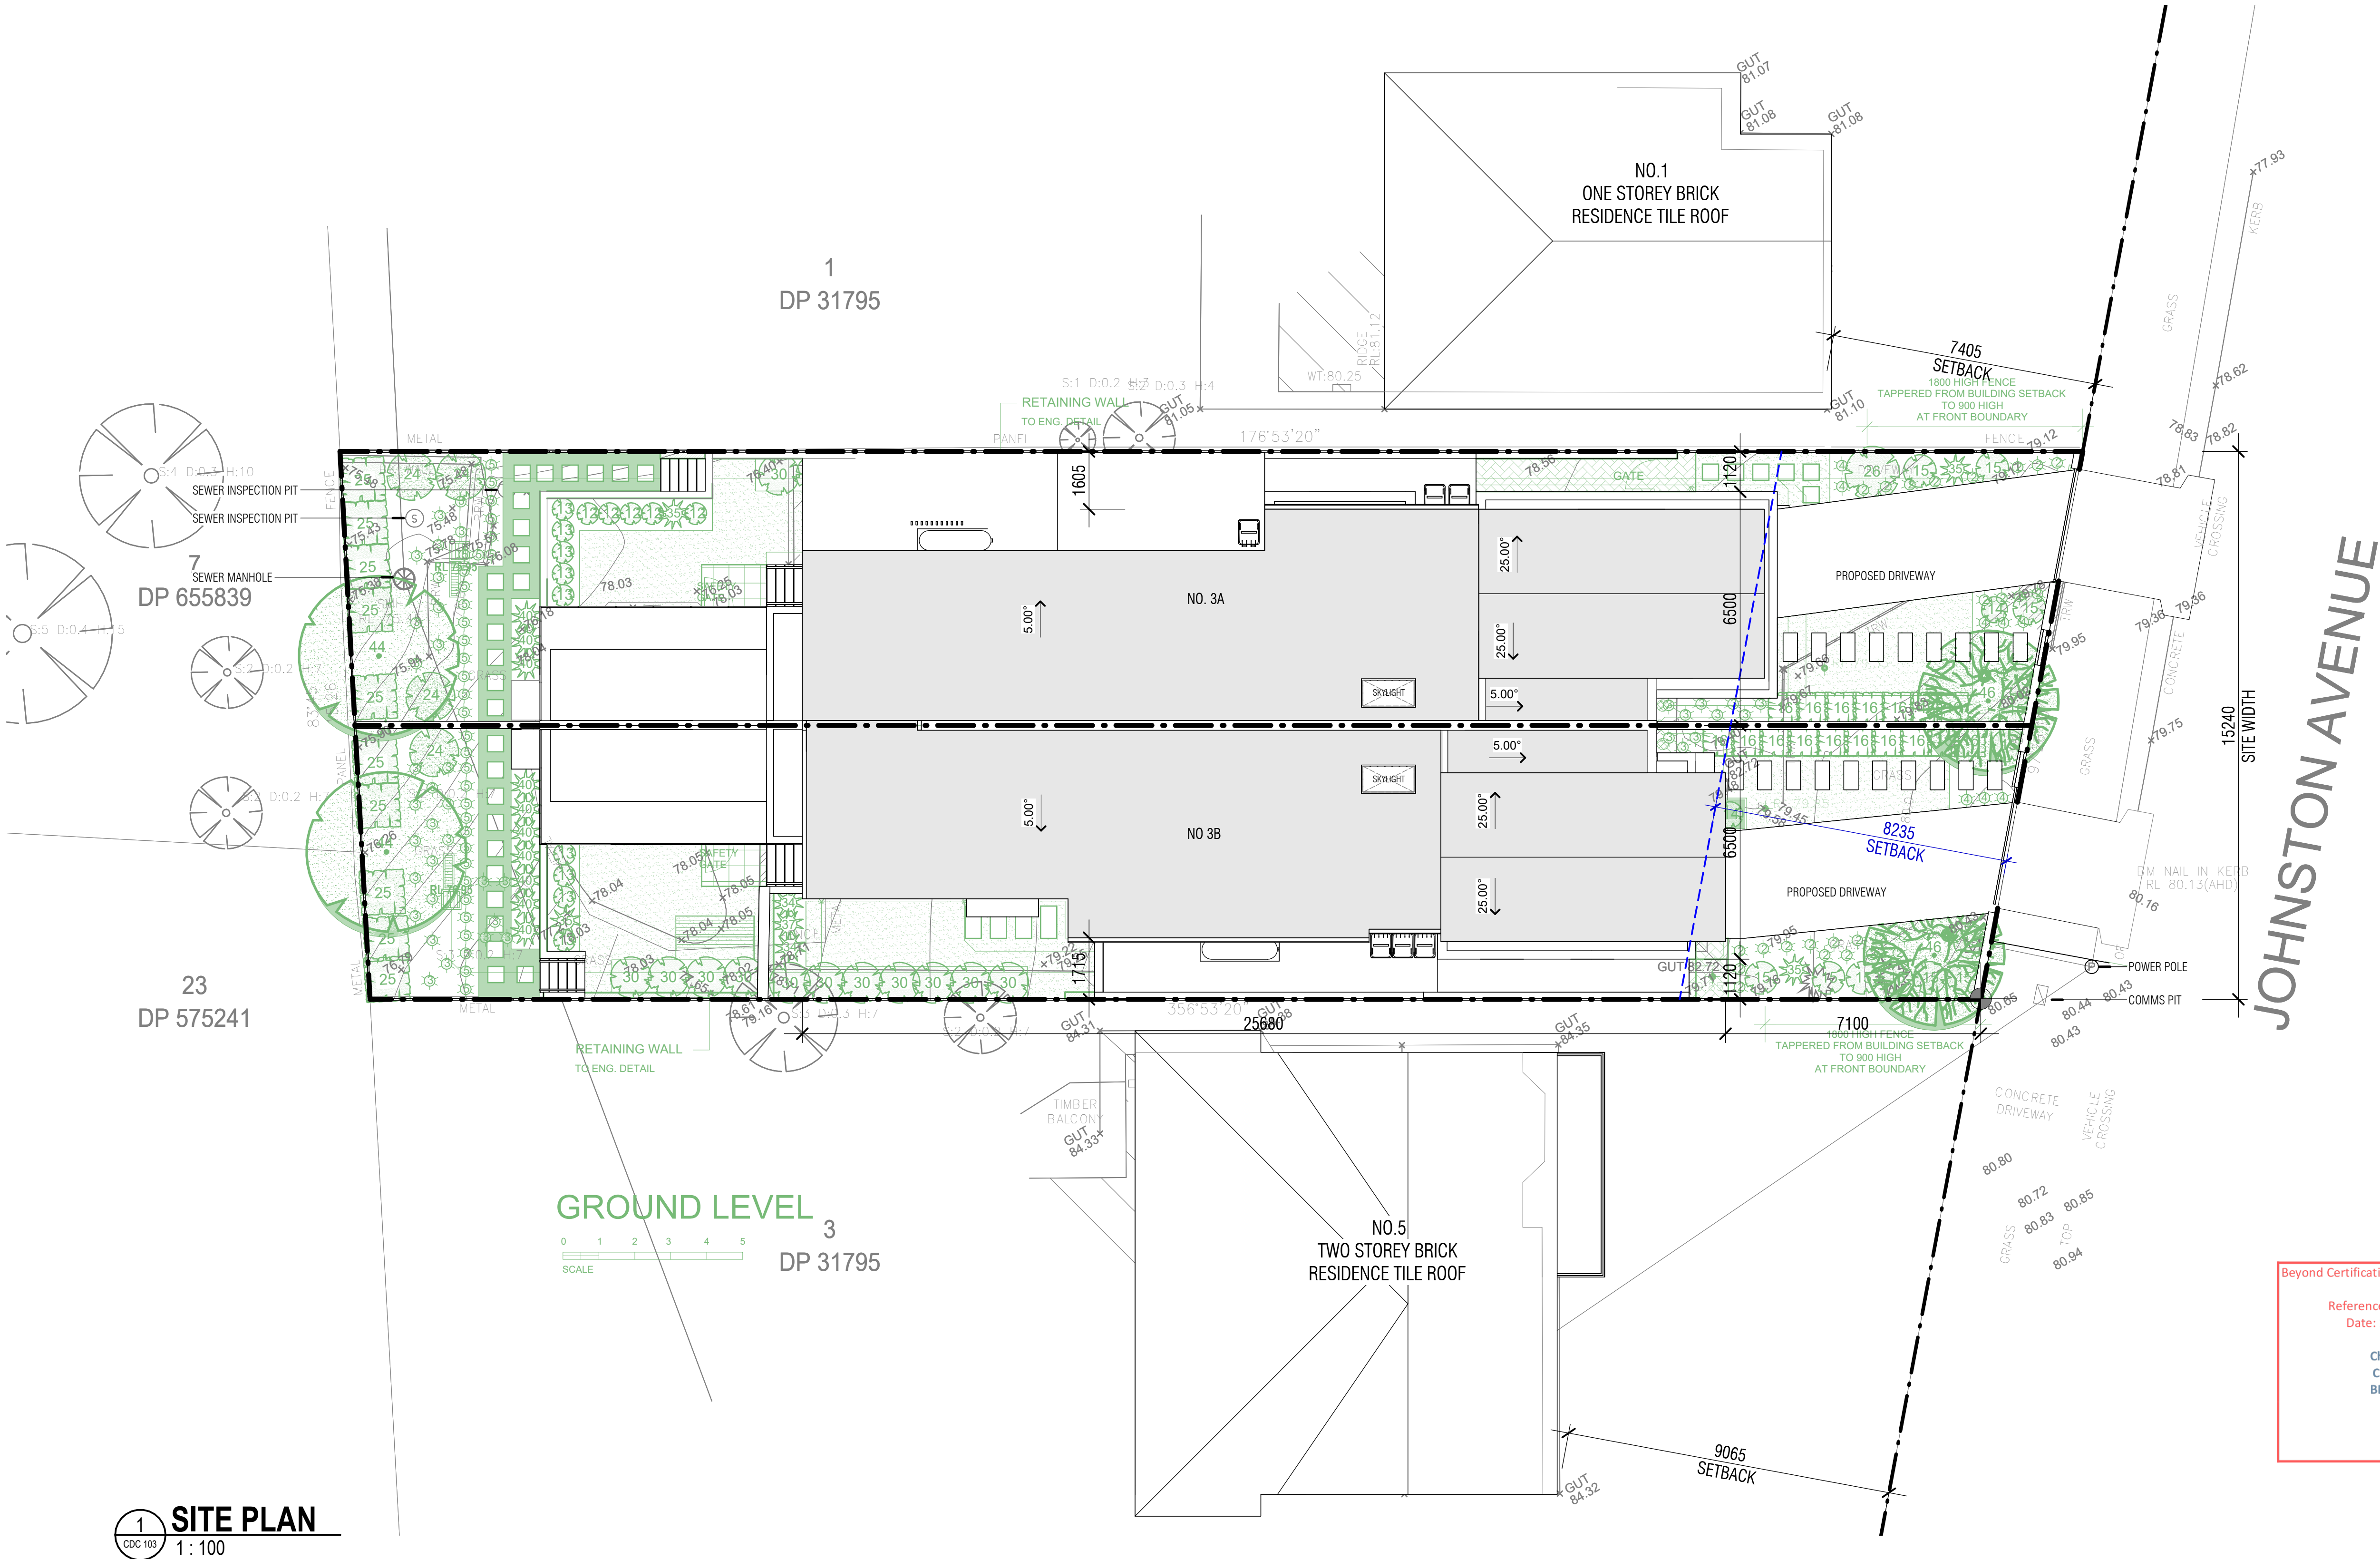

1 SITE PLAN
CDC 103 1 : 100

Beyond Certification (Sonder Projects Pty Ltd)
Reference: 3125176CDC
Date: 17/11/2025

Chen Wu
Certifier
BDC3224

NOTE:
REFER TO LANDSCAPE DRAWING FOR LANDSCAPE DETAIL

COPYRIGHT & GENERAL NOTE:
Figured dimensions shall be taken in preference to scaling. Drawing to be read in conjunction with information on first page. Check all dimensions and levels on site before commencing work or ordering materials. All existing ground lines & trees location are approximate, therefore, to be verified on-site by the builder. Any discrepancies to be verified back to Zhinar Architects before proceeding. All workmanship and materials shall comply with all relevant codes, ordinances, Australian Standards and manufacturers' instructions. Unless noted issued for Construction drawing not to be used for construction. All art / graphic representations are indicative only. Information on this drawing is the copyright of Zhinar Architects. Copying or using this drawing in whole or part without written permission infringes copyright.

C	ISSUE FOR CDC SUBMISSION 3
B	ISSUE FOR CDC SUBMISSION 2
A	ISSUE FOR CDC SUBMISSION
ISSUE	AMENDMENT

7/11/2025	TH	IC
28/10/2025	TH	IC
18/09/2025	TH	IC
DATE	DRAWN	CHECK

Drawing is NOT VALID or issued for use, unless checked


PROJECT ARCHITECTS
IAN CONRY



REGISTRATION NUMBER
NSW No. 8317



TRUE NORTH :

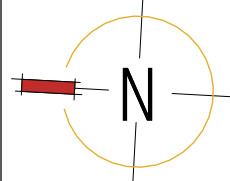

Zhinar Architects Pty Ltd

Suite 1, Level 2
2 Rowe Street
Eastwood, NSW 2122

+61 2 8893 8888 /o
info@zhinar.com.au /e
www.zhinar.com.au /w
28 495 869 790 /abn

PROJECT STATUS :

Complying Development Certificate

PROJECT NAME

Dual Occupancy

3 Johnston Ave

Kirrawee, NSW 2232

L.G.A.: SUTHERLAND SHIRE COUNCIL

SHEET TITLE

SITE PLAN

Checked

Checker

8848

JOB No.


CDC 002

DRAWING No.

SCALE @A1 SHEET
1 : 100

C
ISSUE

scale 1:100 @A1sheet 10

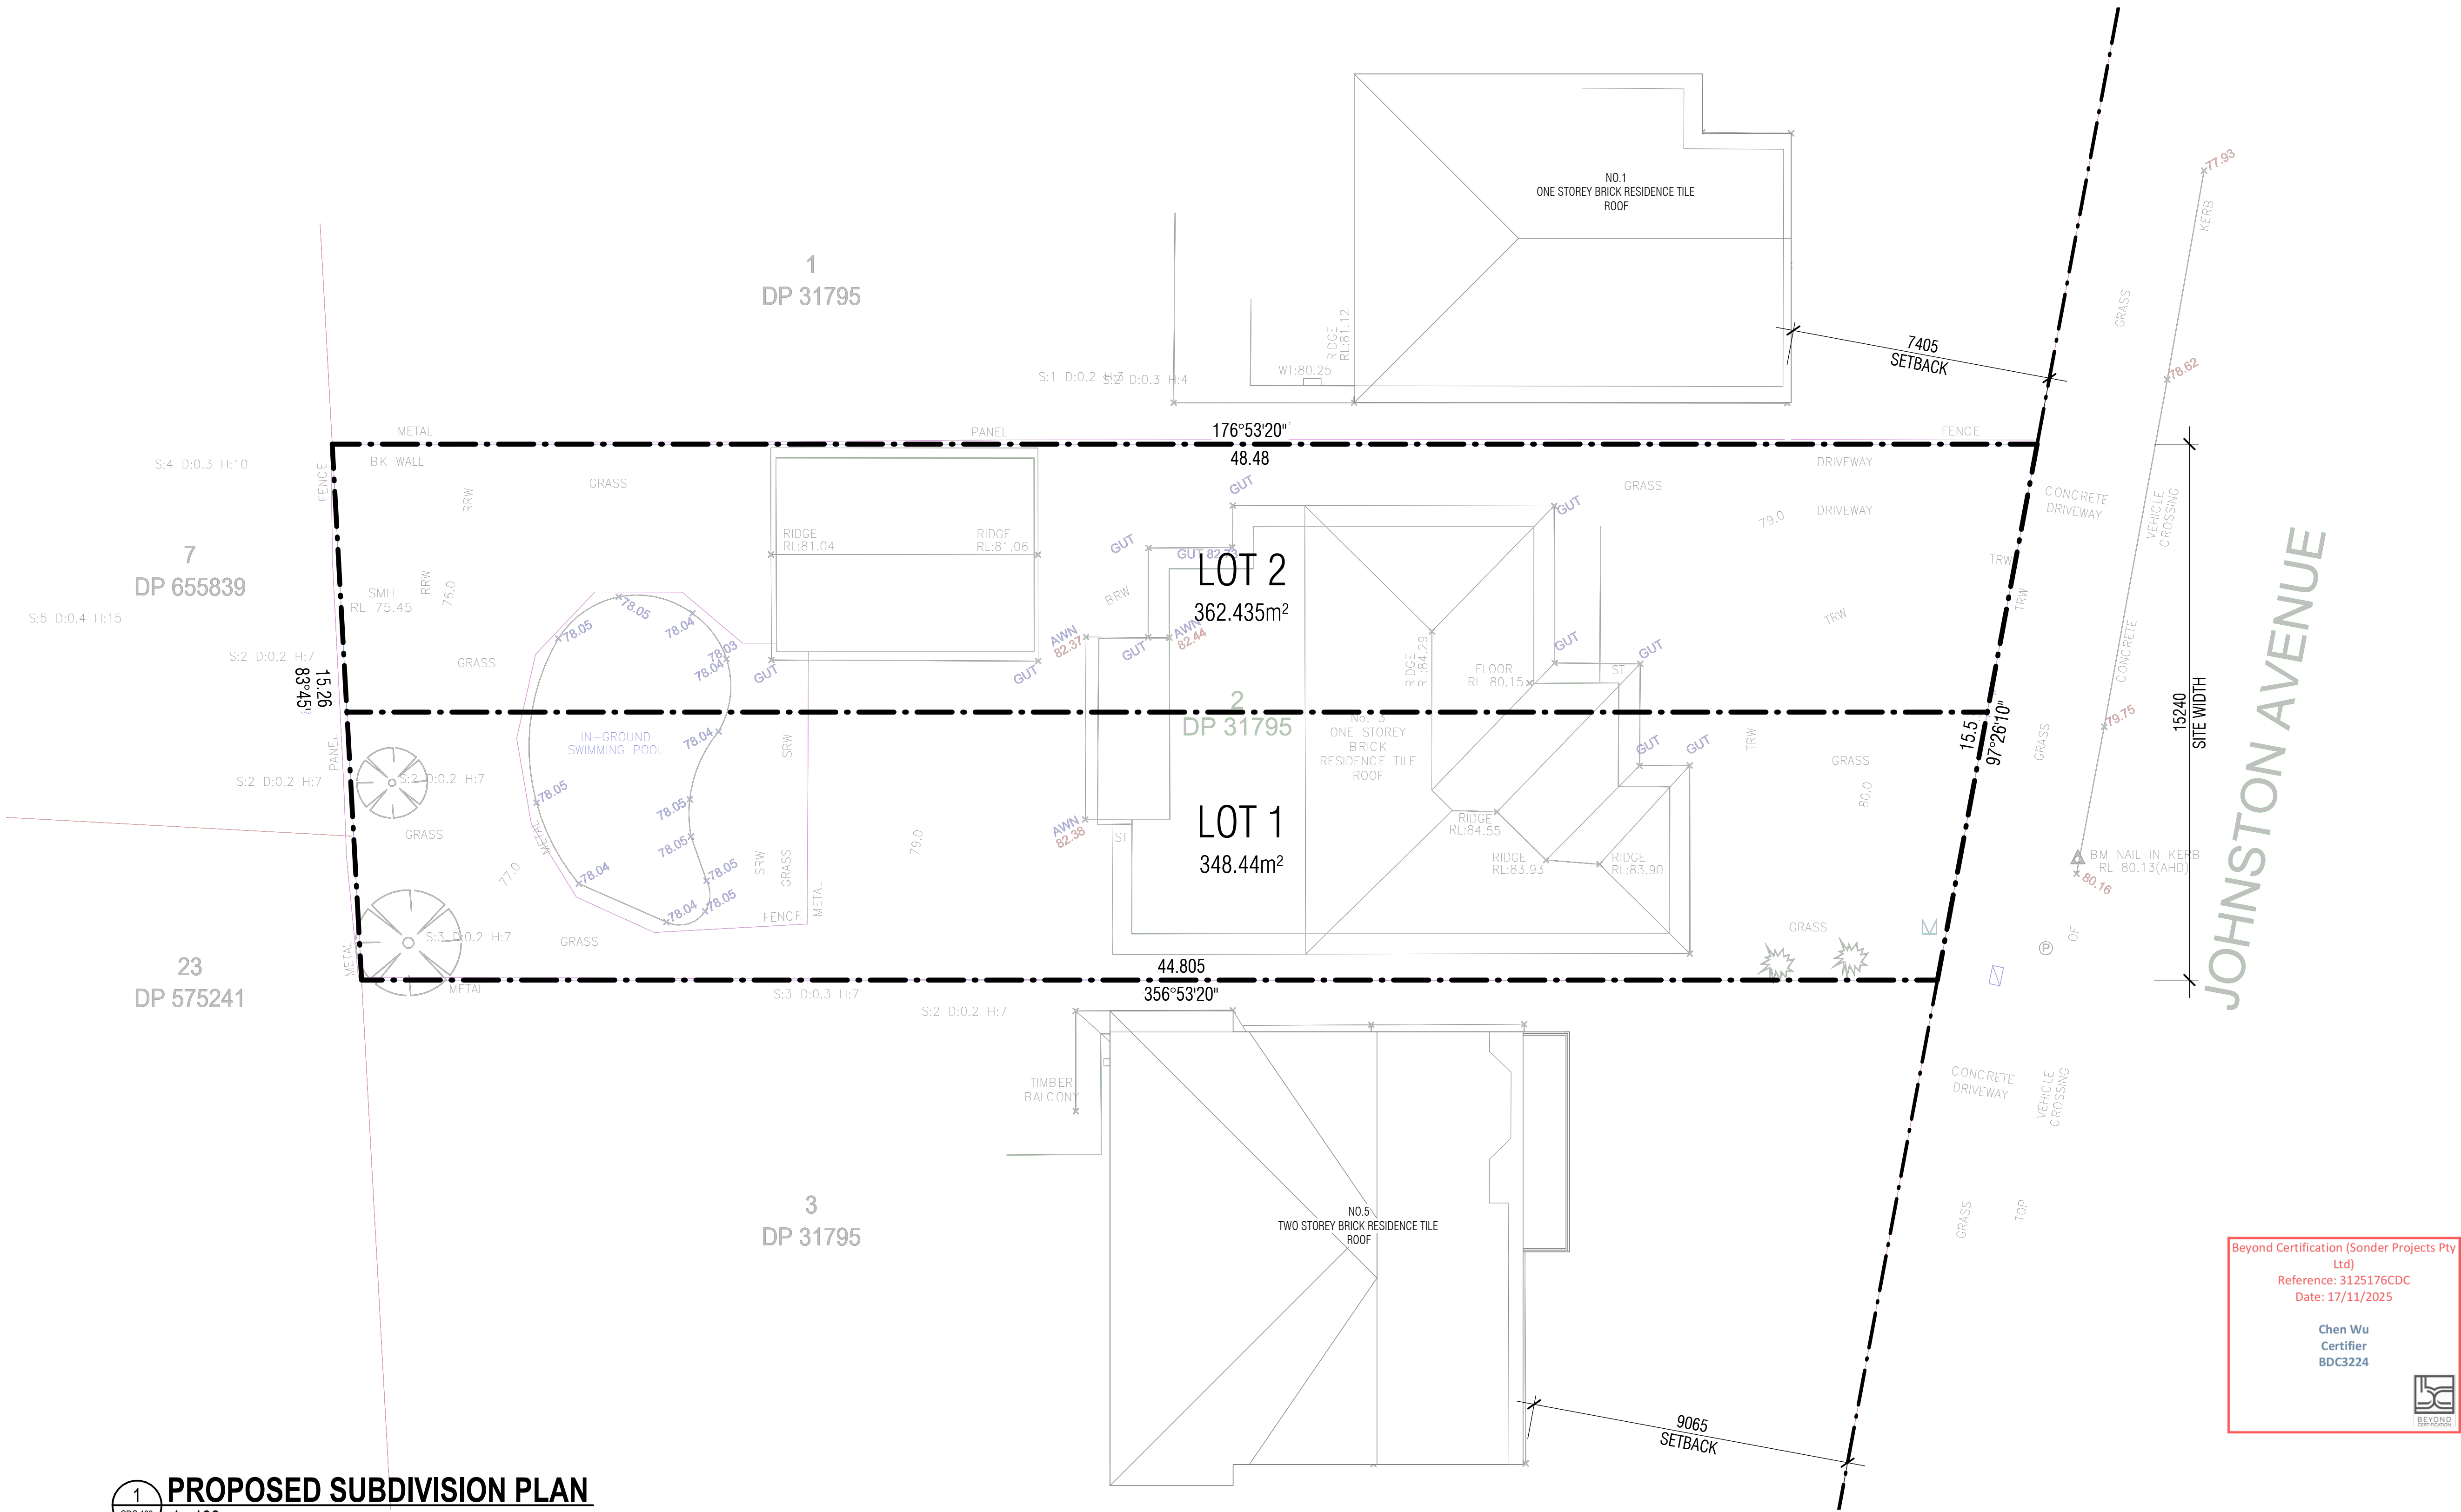

1 PROPOSED SUBDIVISION PLAN
CDC 103 1 : 100

COPYRIGHT & GENERAL NOTE:
Figured dimensions shall be taken in preference to scaling. Drawing to be read in conjunction with information on first page. Check all dimensions and levels on site before commencing work or ordering materials. All existing ground lines & trees location are approximate, therefore, to be verified on-site by the builder. Any discrepancies to be verified back to Zhinar Architects before proceeding. All workmanship and materials shall comply with all relevant codes, ordinances, Australian Standards and manufacturers' instructions. Unless noted issued for Construction drawing not to be used for construction. All art / graphic representations are indicative only. Information on this drawing is the copyright of Zhinar Architects. Copying or using this drawing in whole or part without written permission infringes copyright.

C	ISSUE FOR CDC SUBMISSION 3	7/11/2025	TH	IC
B	ISSUE FOR CDC SUBMISSION 2	28/10/2025	TH	IC
A	ISSUE FOR CDC SUBMISSION	18/09/2025	TH	IC
ISSUE	AMENDMENT	DATE	DRAWN	CHECK

Drawing is NOT VALID or issued for use, unless checked


PROJECT ARCHITECTS
IAN CONRY



REGISTRATION NUMBER
NSW No. 8317



TRUE NORTH :

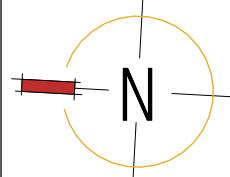

Zhinar Architects Pty Ltd
Suite 1, Level 2
2 Rowe Street
Eastwood, NSW 2122
+61 2 8893 8888 / o
info@zhinar.com.au / e
www.zhinar.com.au / w
28 495 869 790 / abn

PROJECT STATUS :
Complying Development Certificate

PROJECT NAME
Dual Occupancy

3 Johnston Ave
Kirrawee, NSW 2232
LGA: SUTHERLAND SHIRE COUNCIL

SHEET TITLE:
PROPOSED SUBDIVISION PLAN

Checked
Checker


8848
JOB No.

CDC 003
DRAWING No.

SCALE @A1 SHEET
1 : 100

C
ISSUE

scale 1:100 @A1 sheet 10

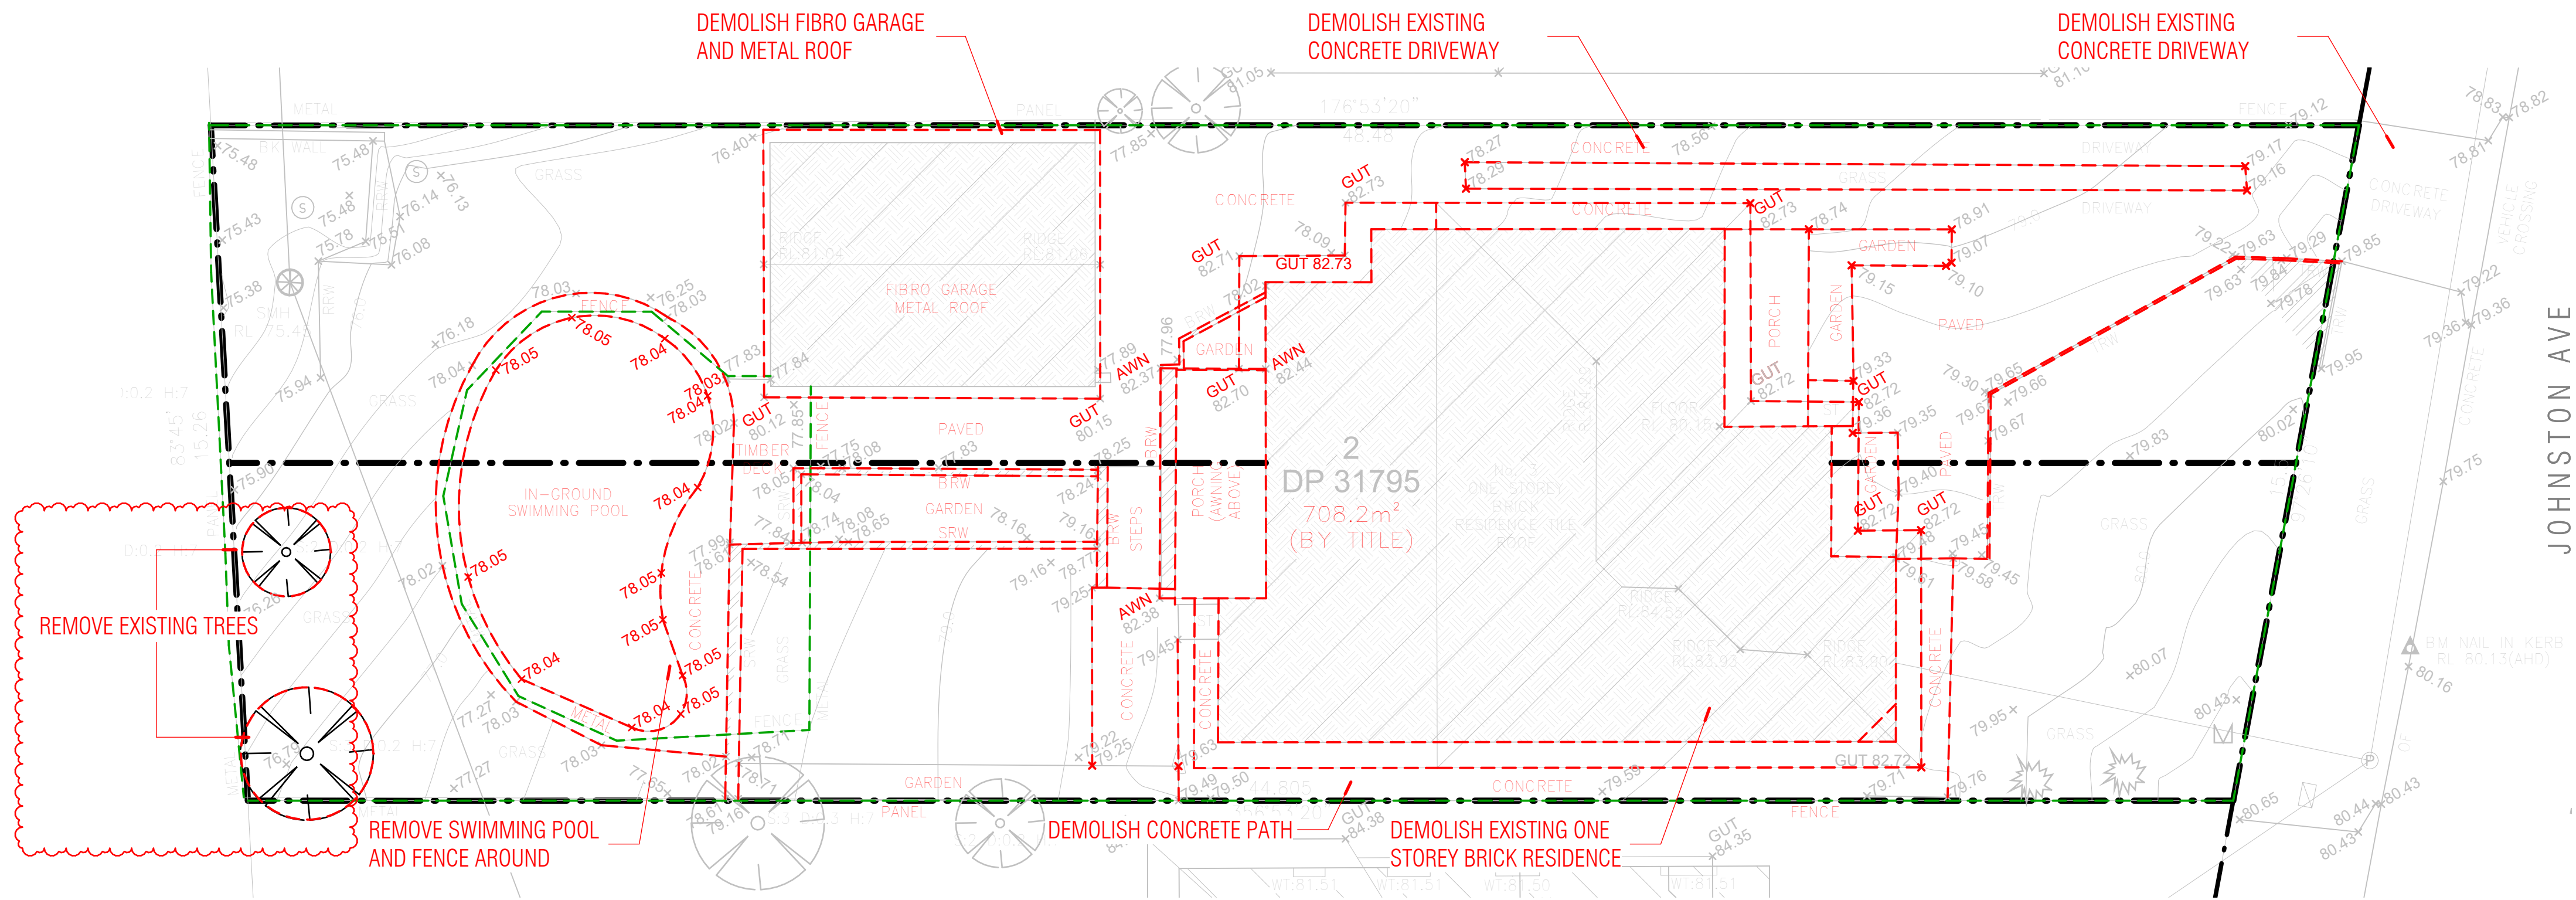

Beyond Certification (Sonder Projects Pty Ltd)
Reference: 3125176CDC
Date: 17/11/2025

Chen Wu
Certifier
BDC3224



1 DEMOLITION PLAN
CDC 103 1 : 100

COPYRIGHT & GENERAL NOTE:
Figured dimensions shall be taken in preference to scaling. Drawing to be read in conjunction with information on first page. Check all dimensions and levels on site before commencing work or ordering materials. All existing ground lines & trees location are approximate, therefore, to be verified on-site by the builder. Any discrepancies to be verified back to Zhinar Architects before proceeding. All workmanship and materials shall comply with all relevant codes, ordinances, Australian Standards and manufacturers' instructions. Unless noted issued for Constructor drawing not to be used for construction. All art / graphic representations are indicative only. Information on this drawing is the copyright of Zhinar Architects. Copying or using this drawing in whole or part without written permission infringes copyright.

C	ISSUE FOR CDC SUBMISSION 3
B	ISSUE FOR CDC SUBMISSION 2
A	ISSUE FOR CDC SUBMISSION
ISSUE	AMENDMENT

7/11/2025	TH	IC
28/10/2025	TH	IC
18/09/2025	TH	IC
DATE	DRAWN	CHECK

Drawing is NOT VALID or issued for use, unless checked


PROJECT ARCHITECTS
IAN CONRY



REGISTRATION NUMBER
NSW No. 8317



TRUE NORTH :

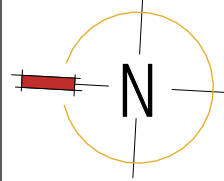

Zhinar Architects Pty Ltd
Suite 1, Level 2
2 Rowe Street
Eastwood, NSW 2122
+61 2 8893 8888 /o
info@zhinar.com.au /e
www.zhinar.com.au /w
28 495 869 790 /abn

PROJECT STATUS :
Complying Development Certificate

PROJECT NAME
Dual Occupancy

3 Johnston Ave
Kirrawee, NSW 2232
L.G.A : SUTHERLAND SHIRE COUNCIL

SHEET TITLE
DEMOLITION

Checked
Checker

8848
JOB No.

CDC 100
DRAWING No.

SCALE @A1 SHEET
1 : 100

C
ISSUE

0 1 2 3 4 5 scale 1:100 @A1sheet 10

CT1	SELECTED CERAMIC TILE
CT2	SELECTED CERAMIC TILE
CPT	SELECTED CARPET
TBR	SELECTED TIMBER FLOOR

UPPER FLOOR PLAN
1:100

GROUND FLOOR PLAN
1:100

The plan shows a rectangular building footprint with various rooms and setbacks. Key features include:

- Rooms:** LIVING/DINING, BED 4, BATH, GARAGE, POOL, ALFRESCO, KITCHEN, DINING TBR, LIVING TBR, BED 4 CPT, BATH CT1, Foyer, Storage, and various closets (CLO).
- Setbacks:** 8235 SETBACK (front), 15225 REAR SETBACK, and 9010 FRONT SETBACK.
- Dimensions:** Overall dimensions are 15240 (width) by 21655 (length). Individual room dimensions are provided throughout the plan.
- Other Features:** EXISTING TREES TO BE REMOVED, EXISTING RETAINING WALL TO BE RETAINED, and various structural notes.

Chen Wu
Certifier
BDC3224

Beyond Certification (Sonder Projects Pty Ltd)
Reference: 3125176CDC
Date: 17/11/2025

C	ISSUE FOR CDC SUBMISSION 3	7/11/2025	TH	IC
B	ISSUE FOR CDC SUBMISSION 2	28/10/2025	TH	IC
A	ISSUE FOR CDC SUBMISSION	18/09/2025	TH	IC
ISSUE	AMENDMENT	DATE	DRAWN	CHE

Drawing is NOT VALID or issued for use, unless checked



Member
Australian
Institute of
Architects

 **DIAL BEFORE
YOU DIG**
www.1100.com.au

+61 2 8893 8888 / p
info@zhinar.com.au / e
www.zhinar.com.au / w
28 495 869 790 / a

Complying Development Certificate


Dual Occupancy

L.G.A.: SUTHERLAND SHIRE COUNCIL

JOB No. **00-40** DRAWING No. **000-10**

IS

CT1	SELECTED CERAMIC TILE
CT2	SELECTED CERAMIC TILE
CPT	SELECTED CARPET
TBR	SELECTED TIMBER FLOOR

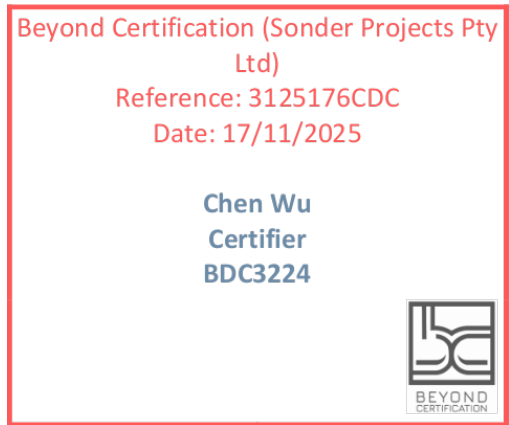

COPYRIGHT & GENERAL NOTE:
 Drawing dimensions shall be taken in preference to scaling. Drawing to be read in conjunction with information on first page. Check all dimensions and levels on site before commencing work or ordering materials. All existing ground lines & trees location are approximate, therefore, to be verified on-site by the builder. Any discrepancy to be verified back to Zhinar Architects before proceeding. All workmanship and materials shall comply with all relevant codes, ordinances, Australian Standards and manufacturers instructions. Unless noted 'Issued for Construction' drawing not to be used for construction. All art / graphic representations are indicative only. Information on this drawing is the copyright of Zhinar Architects. Copying or using this drawing in whole or part without written permission infringes copyright.

C	ISSUE FOR CDC SUBMISSION 3	7/11/2025	TH	IC
B	ISSUE FOR CDC SUBMISSION 2	28/10/2025	TH	IC
A	ISSUE FOR CDC SUBMISSION	18/09/2025	TH	IC
ISSUE	AMENDMENT	DATE	DRAWN	CHECKED

Drawing is NOT VALID or issued for use, unless checked


PROJECT ARCHITECTS
IAN CONRY



REGISTRATION NUMBER
NSW No. 8317



TRUE NORTH :

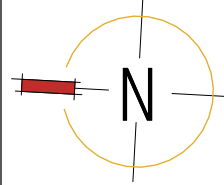

Zhinar Architects Pty Ltd

Suite 1, Level 2
2 Rowe Street
Eastwood, NSW 2122

+61 2 8893 8888 /p
info@zhinar.com.au /e
www.zhinar.com.au /w
28 495 869 790 /abn

PROJECT STATUS :

Complying Development Certificate

PROJECT NAME

PROJECT NAME
Dual Occupancy

3 Johnston Ave

Kirrawee, NSW 2232
L.G.A.: SUTHERLAND SHIRE COUNCIL

SHEET TITLE:

SHEET TITLE:
ROOF PLAN

Checked
Checker

8848 JOB No. CDC 102 DRAWING No.

SCALE @A1 SHEET
1 : 100

C
ISSUE

0 1 2 3 4 5 scale 1:100 @A1 sheet



1 NORTH ELEVATION
CDC 101
1:100



2 SOUTH ELEVATION / STREET ELEVATION
CDC 101
1:100







3 EAST ELEVATION
CDC 101
1:100



4 WEST ELEVATION
CDC 101
1:100

COLOUR & MATERIAL SCHEDULE

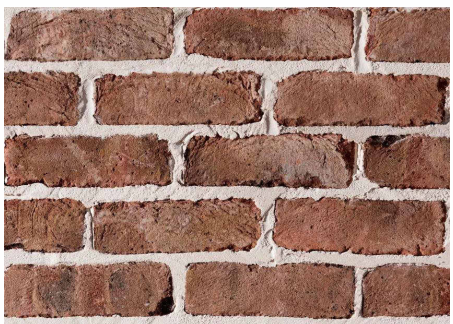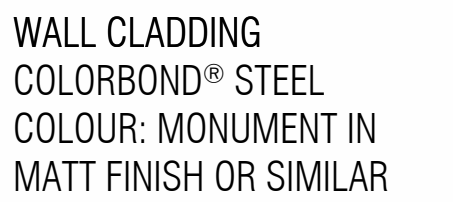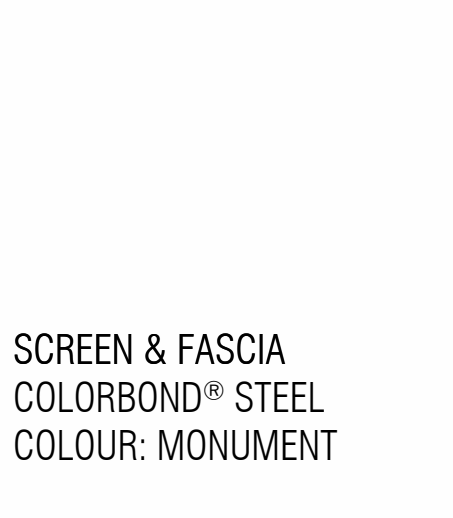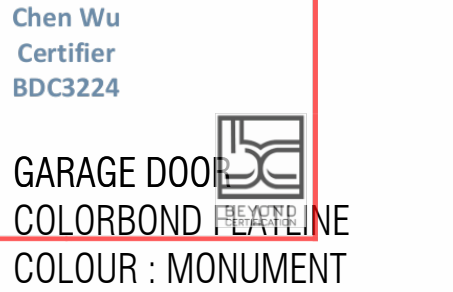01.  MAIN WALL
AUSTRAL BRICKS
SAN SELMO CLASSICO
COLOUR: AGED RED
02.  WALL CLADDING
COLORBOND® STEEL
COLOUR: MONUMENT IN
MATT FINISH OR SIMILAR
03.  BRICK VENEER RENDERED
DULUX
COLOUR : DOMINO OR SIMILAR
04.  SCREEN & FASCIA
COLORBOND® STEEL
COLOUR: MONUMENT
05.  BALCONY CEILING
TAUBMANS
COLOUR : CRISP WHITE OR SIMILAR
06.  GARAGE DOOR
COLORBOND® STEEL
COLOUR : MONUMENT
08.  WINDOWS FRAME- RAILING
COLORBOND
COLOUR: MONUMENT

COPYRIGHT & GENERAL NOTE:
Figured dimensions shall be taken in preference to scaling. Drawing to be read in conjunction with information on first page. Check all dimensions and levels on site before commencing work or ordering materials. All existing ground lines & trees location are approximate, therefore, to be verified on-site by the builder. Any discrepancies to be verified back to Zhihar Architects before proceeding. All workmanship and materials shall comply with all relevant codes, ordinances, Australian Standards and manufacturers' instructions. Unless noted issued for Construction drawing not to be used for construction. All art / graphic representations are indicative only. Information on this drawing is the copyright of Zhihar Architects. Copying or using this drawing in whole or part without written permission infringes copyright.

C	ISSUE FOR CDC SUBMISSION 3	7/11/2025	TH	IC
B	ISSUE FOR CDC SUBMISSION 2	28/10/2025	TH	IC
A	ISSUE FOR CDC SUBMISSION	18/09/2025	TH	IC
ISSUE	AMENDMENT	DATE	DRAWN	CHECK

Drawing is NOT VALID or issued for use, unless checked

PROJECT ARCHITECTS
IAN CONRY



REGISTRATION NUMBER
NSW No. 8317



Zhihar Architects Pty Ltd
Suite 1, Level 2
2 Rowe Street
Eastwood, NSW 2122
~61 2 8893 8888 /o
info@zhihar.com.au /e
www.zhihar.com.au /w
28 495 869 790 /ahn


PROJECT STATUS:
Complying Development Certificate

PROJECT NAME
Dual Occupancy


3 Johnston Ave
Kirrawee, NSW 2232
L.G.A.: SUTHERLAND SHIRE COUNCIL

SHEET TITLE
ELEVATIONS

Checked
Checker
8848
JOB No.
CDC 103
DRAWING No.
SCALE @A1 SHEET
As indicated
C
ISSUE
scale 1:100 @A1 sheet
10

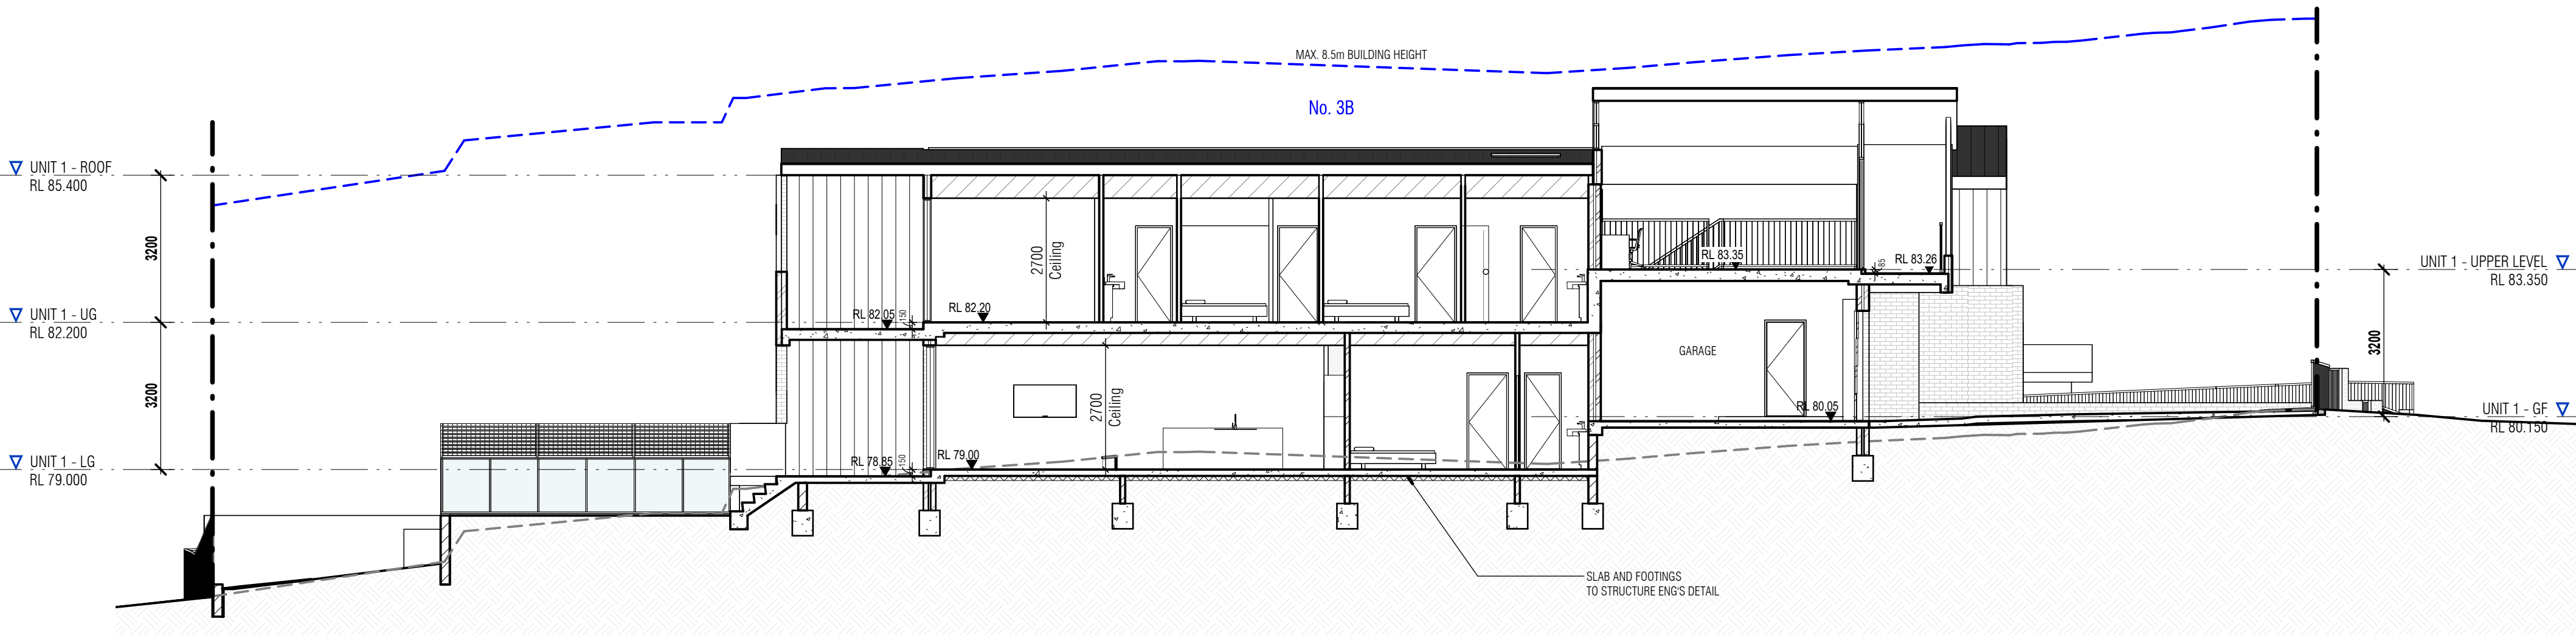

1 SECTION 1
CDC 101
1:100

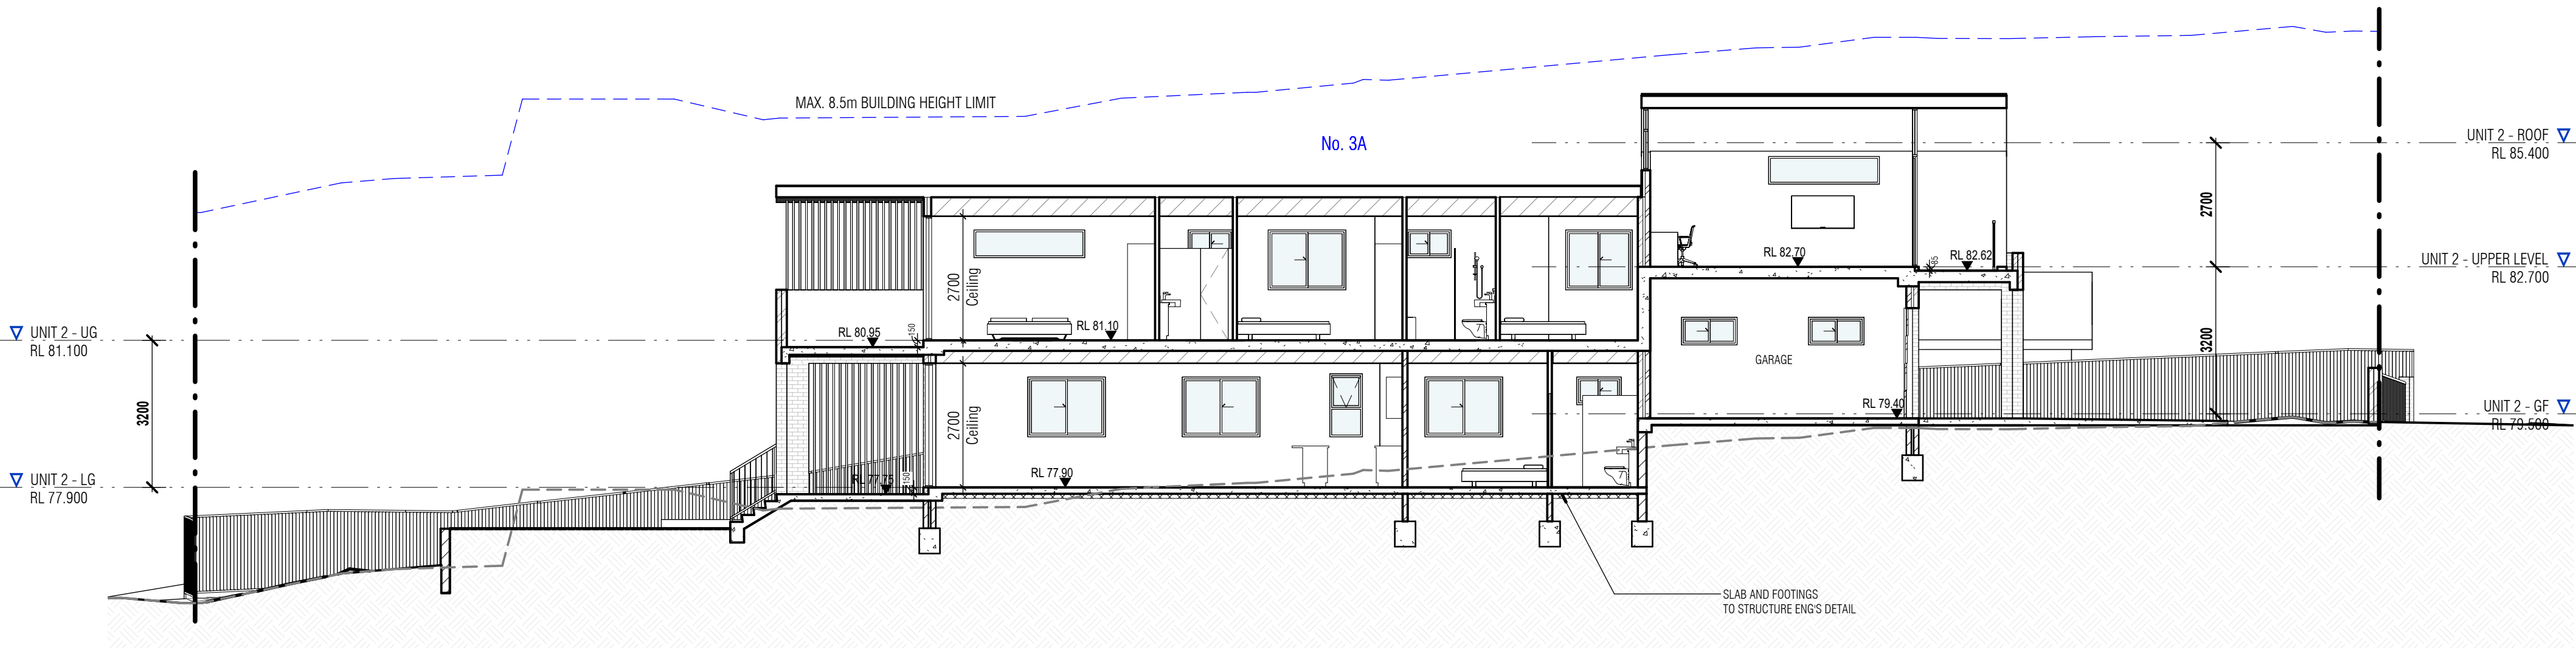

2 SECTION 2
CDC 101
1:100

COPYRIGHT & GENERAL NOTE:
Figured dimensions shall be taken in preference to scaling. Drawing to be read in conjunction with information on first page. Check all dimensions and levels on site before commencing work or ordering materials. All existing ground lines & trees location are approximate, therefore, to be verified on-site by the builder. Any discrepancies to be verified back to Zhinar Architects before proceeding. All workmanship and materials shall comply with all relevant codes, ordinances, Australian Standards and manufacturers' instructions. Unless noted issued for Constructor drawing not to be used for construction. All art / graphic representations are indicative only. Information on this drawing is the copyright of Zhinar Architects. Copying or using this drawing in whole or part without written permission infringes copyright.

C	ISSUE FOR CDC SUBMISSION 3	7/11/2025	TH	IC
B	ISSUE FOR CDC SUBMISSION 2	28/10/2025	TH	IC
A	ISSUE FOR CDC SUBMISSION	18/09/2025	TH	IC
ISSUE	AMENDMENT	DATE	DRAWN	CHECK

Drawing is NOT VALID or issued for use, unless checked

PROJECT ARCHITECTS
IAN CONRY




Member
Architects
Institute of
Architects

REGISTRATION NUMBER
NSW No. 8317



TRUE NORTH :

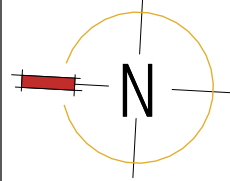

Zhinar Architects Pty Ltd

Suite 1, Level 2
2 Rowe Street
Eastwood, NSW 2122

+61 2 8893 8888 /p
info@zhinar.com.au /e
www.zhinar.com.au /w
28 495 869 790 /dm

PROJECT STATUS :

Complying Development Certificate

PROJECT NAME

Dual Occupancy

3 Johnston Ave

Kirrawee, NSW 2232

L.G.A.: SUTHERLAND SHIRE COUNCIL

SHEET TITLE

SECTIONS

Checked

Checker

8848

JOB No.

CDC 104

DRAWING No.

SCALE @A1 SHEET

1:100

C

ISSUE

0 1 2 3 4 5 scale 1:100 @A1sheet 10



NOTE: REFER TO STRUCTURE ENGINEER'S DRAWING FOR MORE DETAIL



7/11/2025	TH	IC
28/10/2025	TH	IC
18/09/2025	TH	IC
DATE	DRAWN	CHE


Drawing is NOT VALID or issued for use, unless checked



Member
Australian
Institute of
Architects

 **DIAL BEFORE
YOU DIG**
www.1100.com.au

100

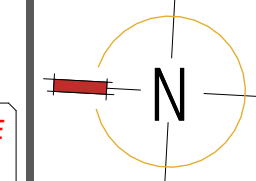

+61 2 8893 8888
info@zhinar.com.au
www.zhinar.com.au
28 495 869 790

Comply

Complying Development Certificate


Dual Oc

Dual Occupancy

L.G.A: SUTHERLAND SHIRE COUNCIL



2 GROUND FLOOR PLAN
1: 100

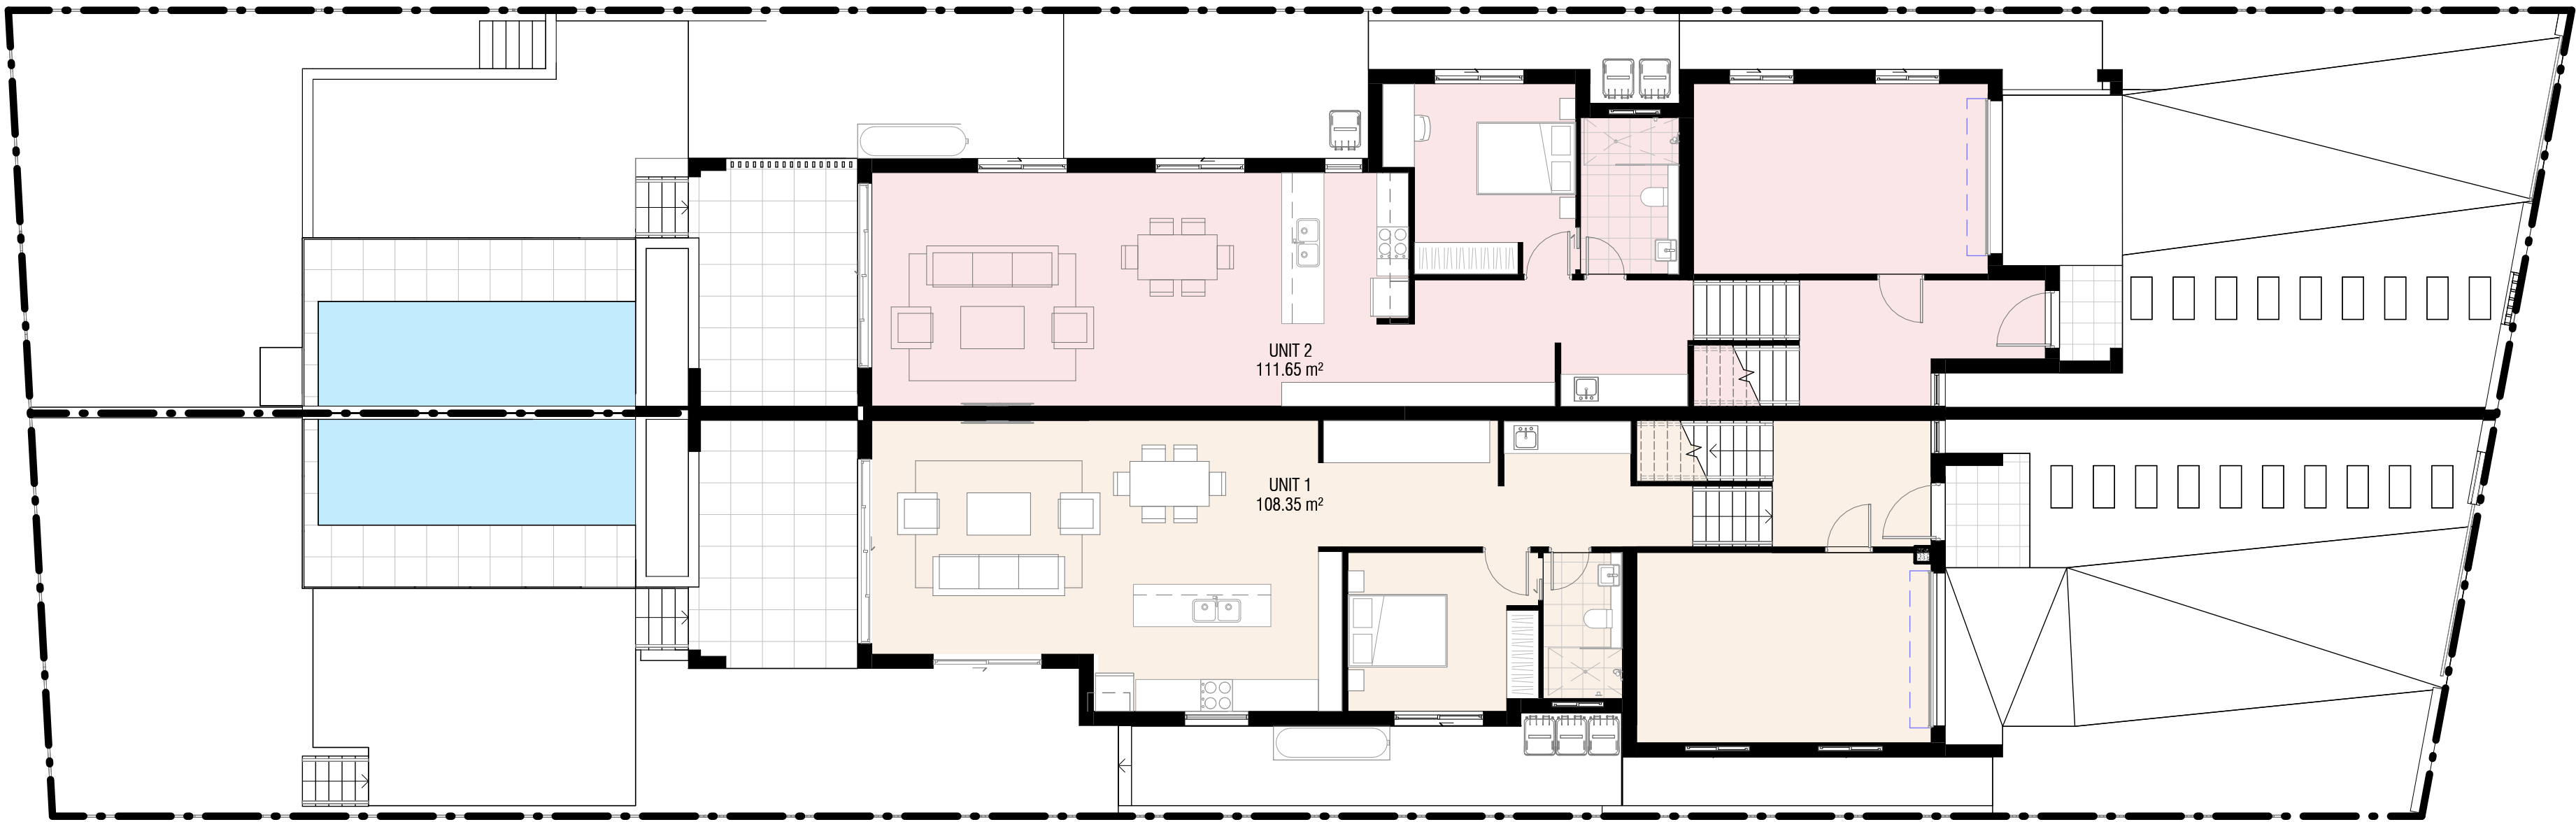

Area Schedule (FSR)	
Name	Area
UNIT 1	100.5 m²
UNIT 1	108.3 m²

UNIT 2	100.8 m²
UNIT 2	111.7 m²
	421.2 m²

PROPOSED	
Unit 1 GFA	= 208.8 m²
Unit 2 GFA	= 212.5 m²
TOTAL GFA	= 421.3 m²

3 UPPER FLOOR PLAN
1: 100



UNIT 1
UNIT 2

1 FLOOR PLAN
1: 100



Area Schedule (LANDSCAPE)		
Name	Level	Area

FRONT LANDSCAPE	UNIT 1 - LG	15.6 m²
FRONT LANDSCAPE	UNIT 1 - LG	4.6 m²
FRONT LANDSCAPE	UNIT 1 - LG	24.4 m²
FRONT LANDSCAPE	UNIT 1 - LG	20.4 m²
FRONT LANDSCAPE		65.0 m²
LANDSCAPE	UNIT 1 - LG	18.5 m²
LANDSCAPE	UNIT 1 - LG	23.8 m²
LANDSCAPE	UNIT 1 - LG	7.1 m²
LANDSCAPE		49.4 m²
REAR LANDSCAPE	UNIT 1 - LG	39.3 m²
REAR LANDSCAPE	UNIT 1 - LG	30.9 m²
REAR LANDSCAPE	UNIT 1 - LG	36.3 m²
REAR LANDSCAPE	UNIT 1 - LG	23.8 m²
REAR LANDSCAPE	UNIT 1 - LG	11.2 m²
REAR LANDSCAPE		141.4 m²
Grand total		255.8 m²

COPYRIGHT & GENERAL NOTE:
Figured dimensions shall be taken in preference to scaling. Drawing to be read in conjunction with information on first page. Check all dimensions and levels on site before commencing work or ordering materials. All existing ground lines & trees location are approximate, therefore, to be verified on-site by the builder. Any discrepancies to be verified back to Zhinar Architects before proceeding. All workmanship and materials shall comply with all relevant codes, ordinances, Australian Standards and manufacturers' instructions. Unless noted issued for Construction drawing not to be used for construction. All art / graphic representations are indicative only. Information on this drawing is the copyright of Zhinar Architects. Copying or using this drawing in whole or part without written permission infringes copyright.

C	ISSUE FOR CDC SUBMISSION 3	7/11/2025	TH	IC
B	ISSUE FOR CDC SUBMISSION 2	28/10/2025	TH	IC
A	ISSUE FOR CDC SUBMISSION	18/09/2025	TH	IC
ISSUE	AMENDMENT	DATE	DRAWN	CHECK

Drawing is NOT VALID or issued for use, unless checked


PROJECT ARCHITECTS
IAN CONRY



REGISTRATION NUMBER
NSW No. 8317



TRUE NORTH :

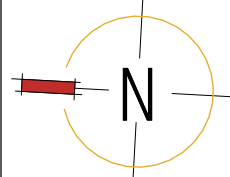

Zhinar Architects Pty Ltd
Suite 1, Level 2
2 Rowe Street
Eastwood, NSW 2122

+61 2 8893 8888 / o
info@zhinar.com.au / e
www.zhinar.com.au / w
28 495 869 790 / abn

PROJECT STATUS :
Complying Development Certificate

PROJECT NAME
Dual Occupancy

3 Johnston Ave
Kirrawee, NSW 2232
L.G.A.: SUTHERLAND SHIRE COUNCIL

SHEET TITLE:
AREA CALCULATIONS


Checked
Checker

8848
JOB No. CDC 200
DRAWING No.

SCALE @A1 SHEET
1 : 100

C
ISSUE

scale 1:100 @A1sheet 10

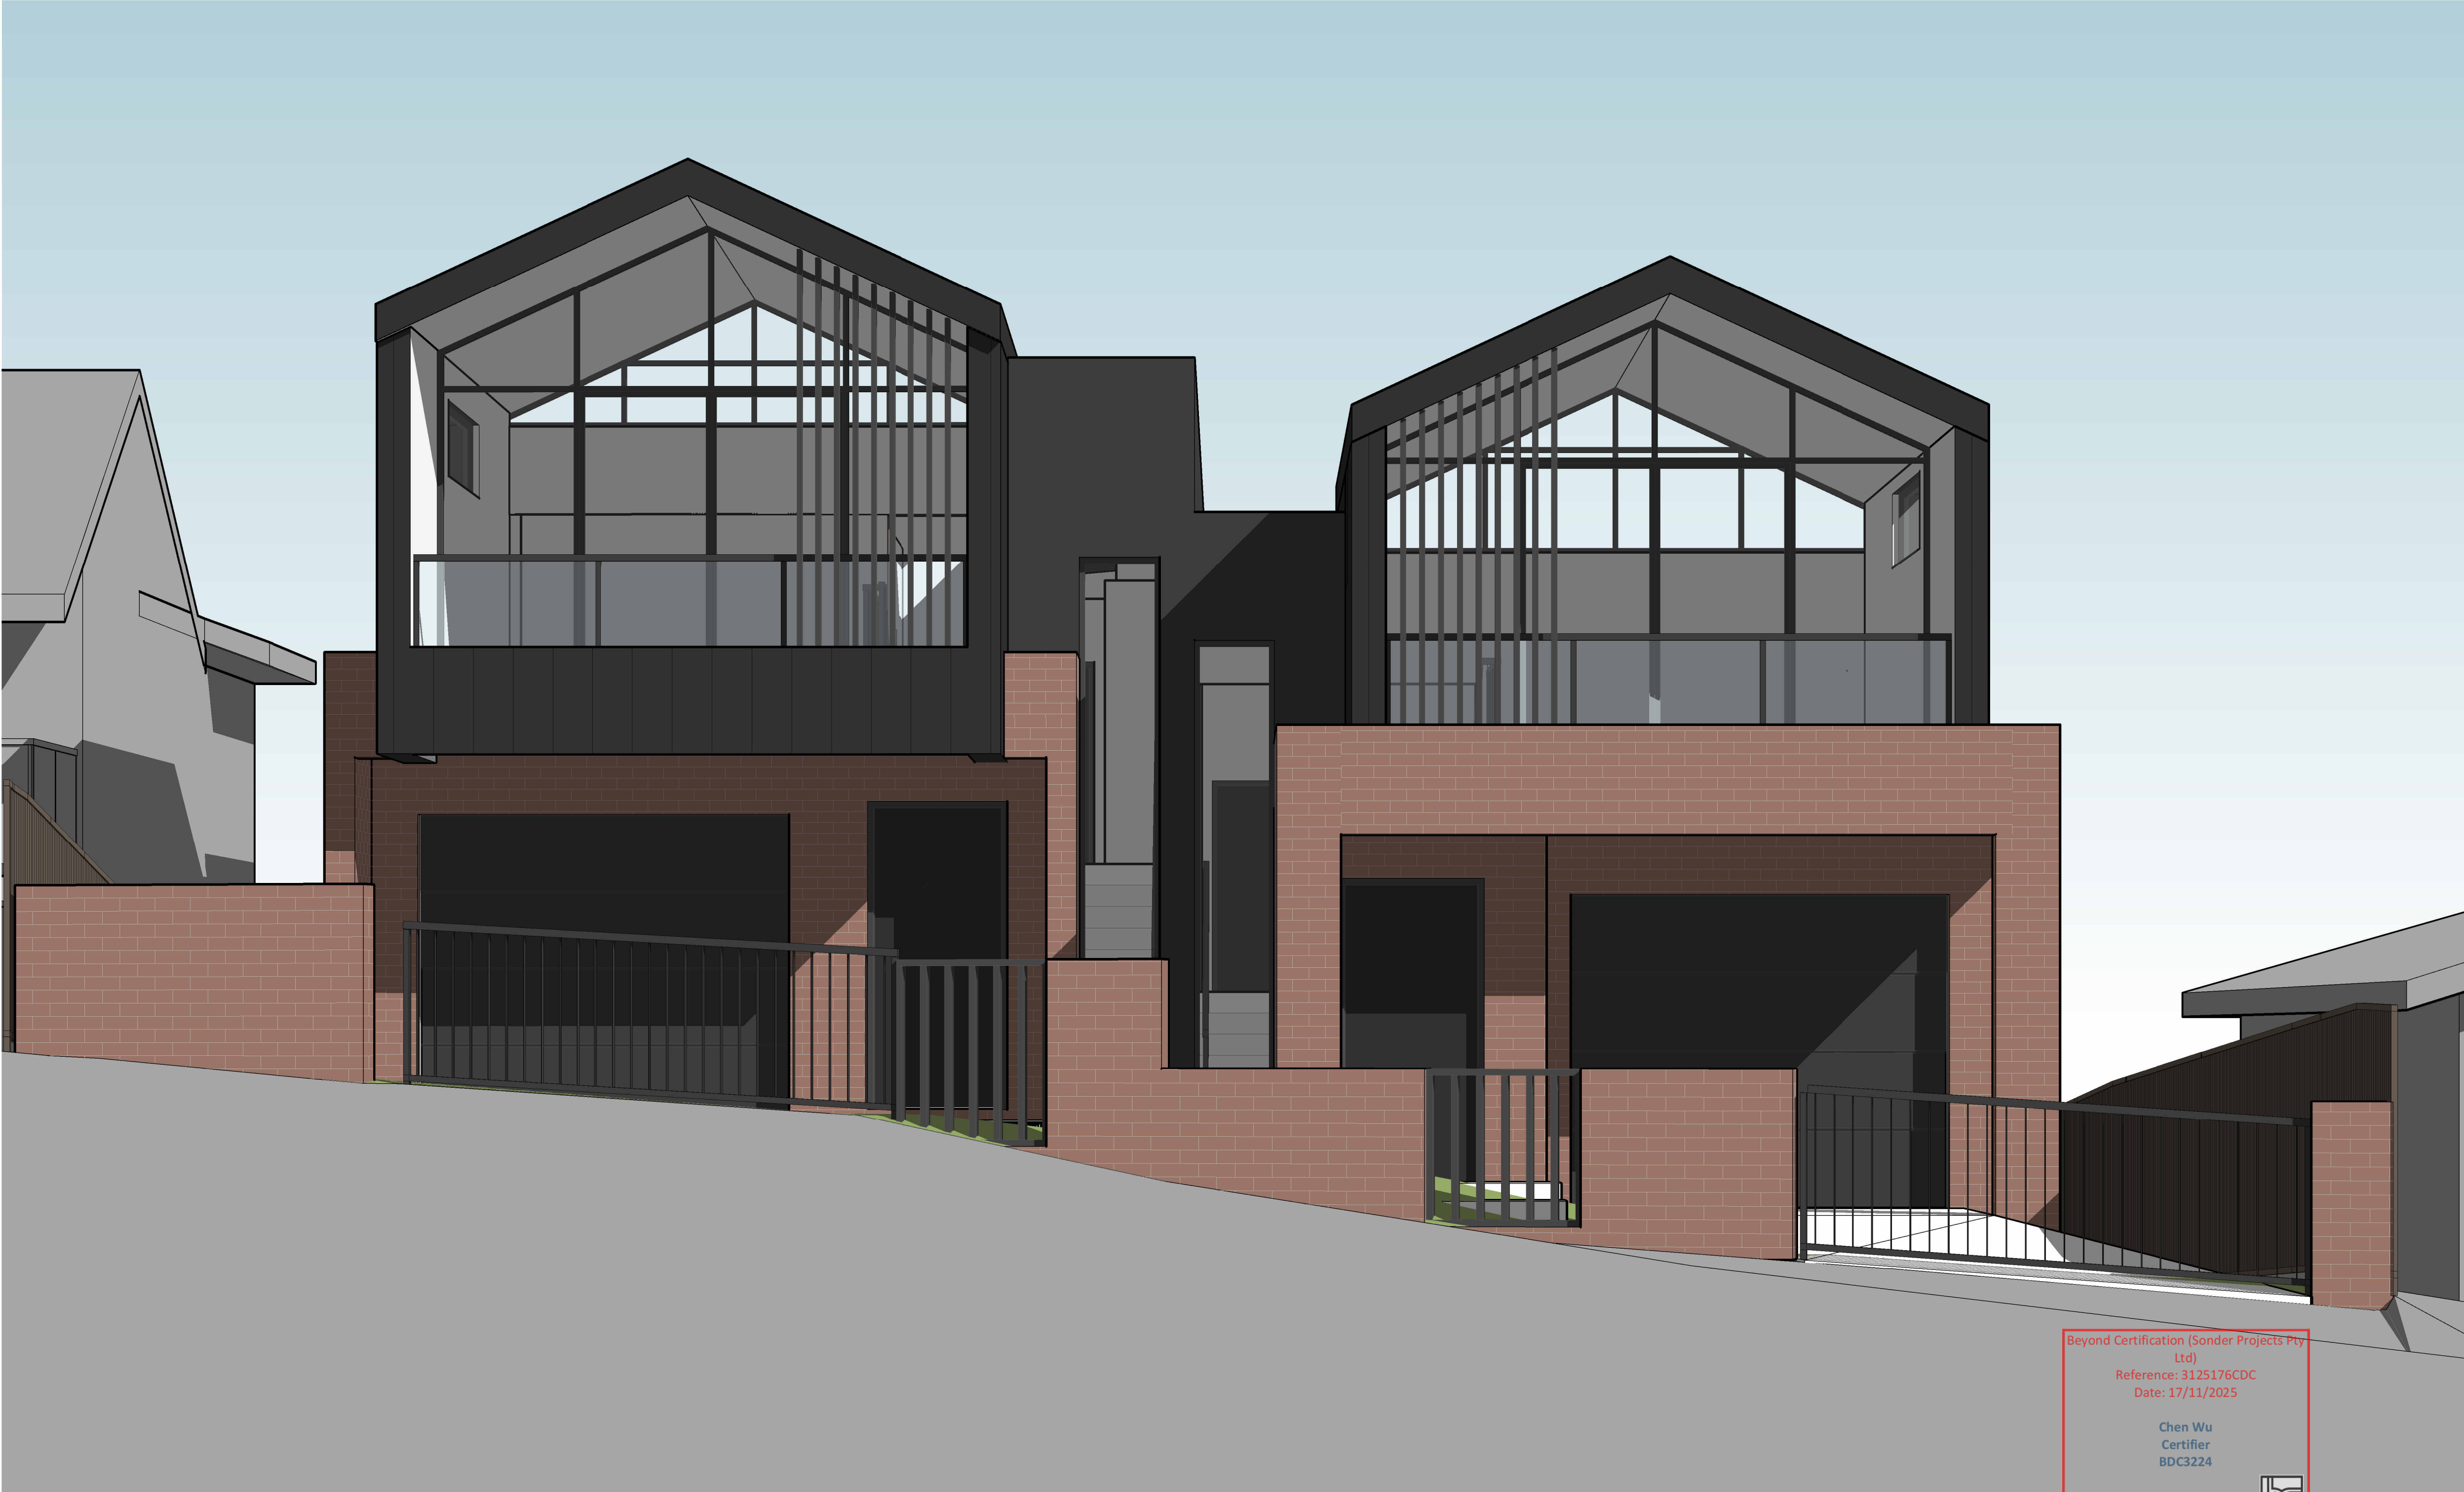

3D PERSPECTIVE FRONT

COPYRIGHT & GENERAL NOTE:
Figured dimensions shall be taken in preference to scaling. Drawing to be read in conjunction with information on first page. Check all dimensions and levels on site before commencing work or ordering materials. All existing ground lines & levels/location are approximate, therefore, to be verified on-site by the builder. Any discrepancies to be verified back to Zhinar Architects before proceeding. All workmanship and materials shall comply with all relevant codes, ordinances, Australian Standards and manufacturers' instructions. Unless noted issued for Construction drawing not to be used for construction. All art / graphic representations are indicative only. Information on this drawing is the copyright of Zhinar Architects. Copying or using this drawing in whole or part without written permission infringes copyright.

C	ISSUE FOR CDC SUBMISSION 3
B	ISSUE FOR CDC SUBMISSION 2
A	ISSUE FOR CDC SUBMISSION
ISSUE	AMENDMENT

7/11/2025	TH	IC
28/10/2025	TH	IC
18/09/2025	TH	IC
DATE	DRAWN	CHECK

Drawing is NOT VALID or issued for use, unless checked

PROJECT ARCHITECTS
IAN CONRY



REGISTRATION NUMBER
NSW No. 8317



Zhinar Architects Pty Ltd
Suite 1, Level 2
2 Rowe Street
Eastwood, NSW 2122
+61 2 8893 8888 /p
info@zhinar.com.au /e
www.zhinar.com.au /w
28 495 869 790 /dn

PROJECT STATUS:
Complying Development Certificate

PROJECT NAME
Dual Occupancy

3 Johnston Ave
Kirrawee, NSW 2232
L.G.A.: SUTHERLAND SHIRE COUNCIL

SHEET TITLE
3D PERSPECTIVE 1

Checked
Checker
8848
JOB No.
CDC 300
DRAWING No.
scale 1:100 @A1 sheet
SCALE @A1 SHEET
C
ISSUE



3D PERSPECTIVE REAR

Beyond Certification (Sonder Projects Pty Ltd)
Reference: 3125176CDC
Date: 17/11/2025

Chen Wu
Certifier
BDC3224



COPYRIGHT & GENERAL NOTE:
Figured dimensions shall be taken in preference to scaling. Drawing to be read in conjunction with information on first page. Check all dimensions and levels on site before commencing work or ordering materials. All existing ground lines & trees location are approximate, therefore, to be verified on-site by the builder. Any discrepancies to be verified back to Zhinar Architects before proceeding. All workmanship and materials shall comply with all relevant codes, ordinances, Australian Standards and manufacturers' instructions. Unless noted issued for Construction drawing not to be used for construction. All art / graphic representations are indicative only. Information on this drawing is the copyright of Zhinar Architects. Copying or using this drawing in whole or part without written permission infringes copyright.

C	ISSUE FOR CDC SUBMISSION 3
B	ISSUE FOR CDC SUBMISSION 2
A	ISSUE FOR CDC SUBMISSION
ISSUE	AMENDMENT

7/11/2025	TH	IC
28/10/2025	TH	IC
18/09/2025	TH	IC
DATE	DRAWN	CHECK

Drawing is NOT VALID or issued for use, unless checked

PROJECT ARCHITECTS
IAN CONRY



REGISTRATION NUMBER
NSW No. 8317



Zhinar Architects Pty Ltd
Suite 1, Level 2
2 Rowe Street
Eastwood, NSW 2122
+61 2 8893 8888 /p
info@zhinar.com.au /e
www.zhinar.com.au /w
28 495 869 790 /abn

PROJECT STATUS:
Complying Development Certificate

PROJECT NAME
Dual Occupancy

3 Johnston Ave
Kirrawee, NSW 2232
L.G.A.: SUTHERLAND SHIRE COUNCIL

SHEET TITLE
3D PERSPECTIVE 2

Checked
Checker

8848
JOB No.


CDC 301
DRAWING No.

SCALE @A1 SHEET

C
ISSUE

0 1 2 3 4 5 scale 1:100 @A1 sheet 10


DOOR SCHEDULE					
Mark	Type Mark	Height	Width	Description	Type Comments
A1	A	2400	1090	TIMBER	
A2	B	2400	2890	PCA	
A3	C	2100	900	TMB	
A6	F	2100	800	TMB	
A7	C	2100	900	TMB	
A8	G	2060	800	TMB	SLIDING DOOR
A10	H	2700	3490	PCA	4 PANELS STACKED
A11	I	2400	1030	PCA	
A11	I	2400	1030	PCA	
A12	F	2100	800	TMB	
A13	C	2100	900	TMB	
A14	C	2100	900	TMB	
A15	C	2100	900	TMB	
A16	F	2100	800	TMB	
A17	K	2700	3200	PCA	3 PANELS STACKED
B1	A	2400	1090	TIMBER	
B2	B	2400	2890	PCA	
B3	C	2100	900	TMB	
B6	F	2100	800	TMB	
B7	C	2100	900	TMB	
B8	G	2060	800	TMB	SLIDING DOOR
B9	L	2700	2050	PCA	2 PANELS SLIDING
B10	H	2700	3490	PCA	4 PANELS STACKED
B11	J	2400	1030	PCA	
B11	J	2400	1030	PCA	
B12	F	2100	800	TMB	
B13	C	2100	900	TMB	
B14	C	2100	900	TMB	
B15	C	2100	900	TMB	
B16	F	2100	800	TMB	
B17	K	2700	3200	PCA	3 PANELS STACKED

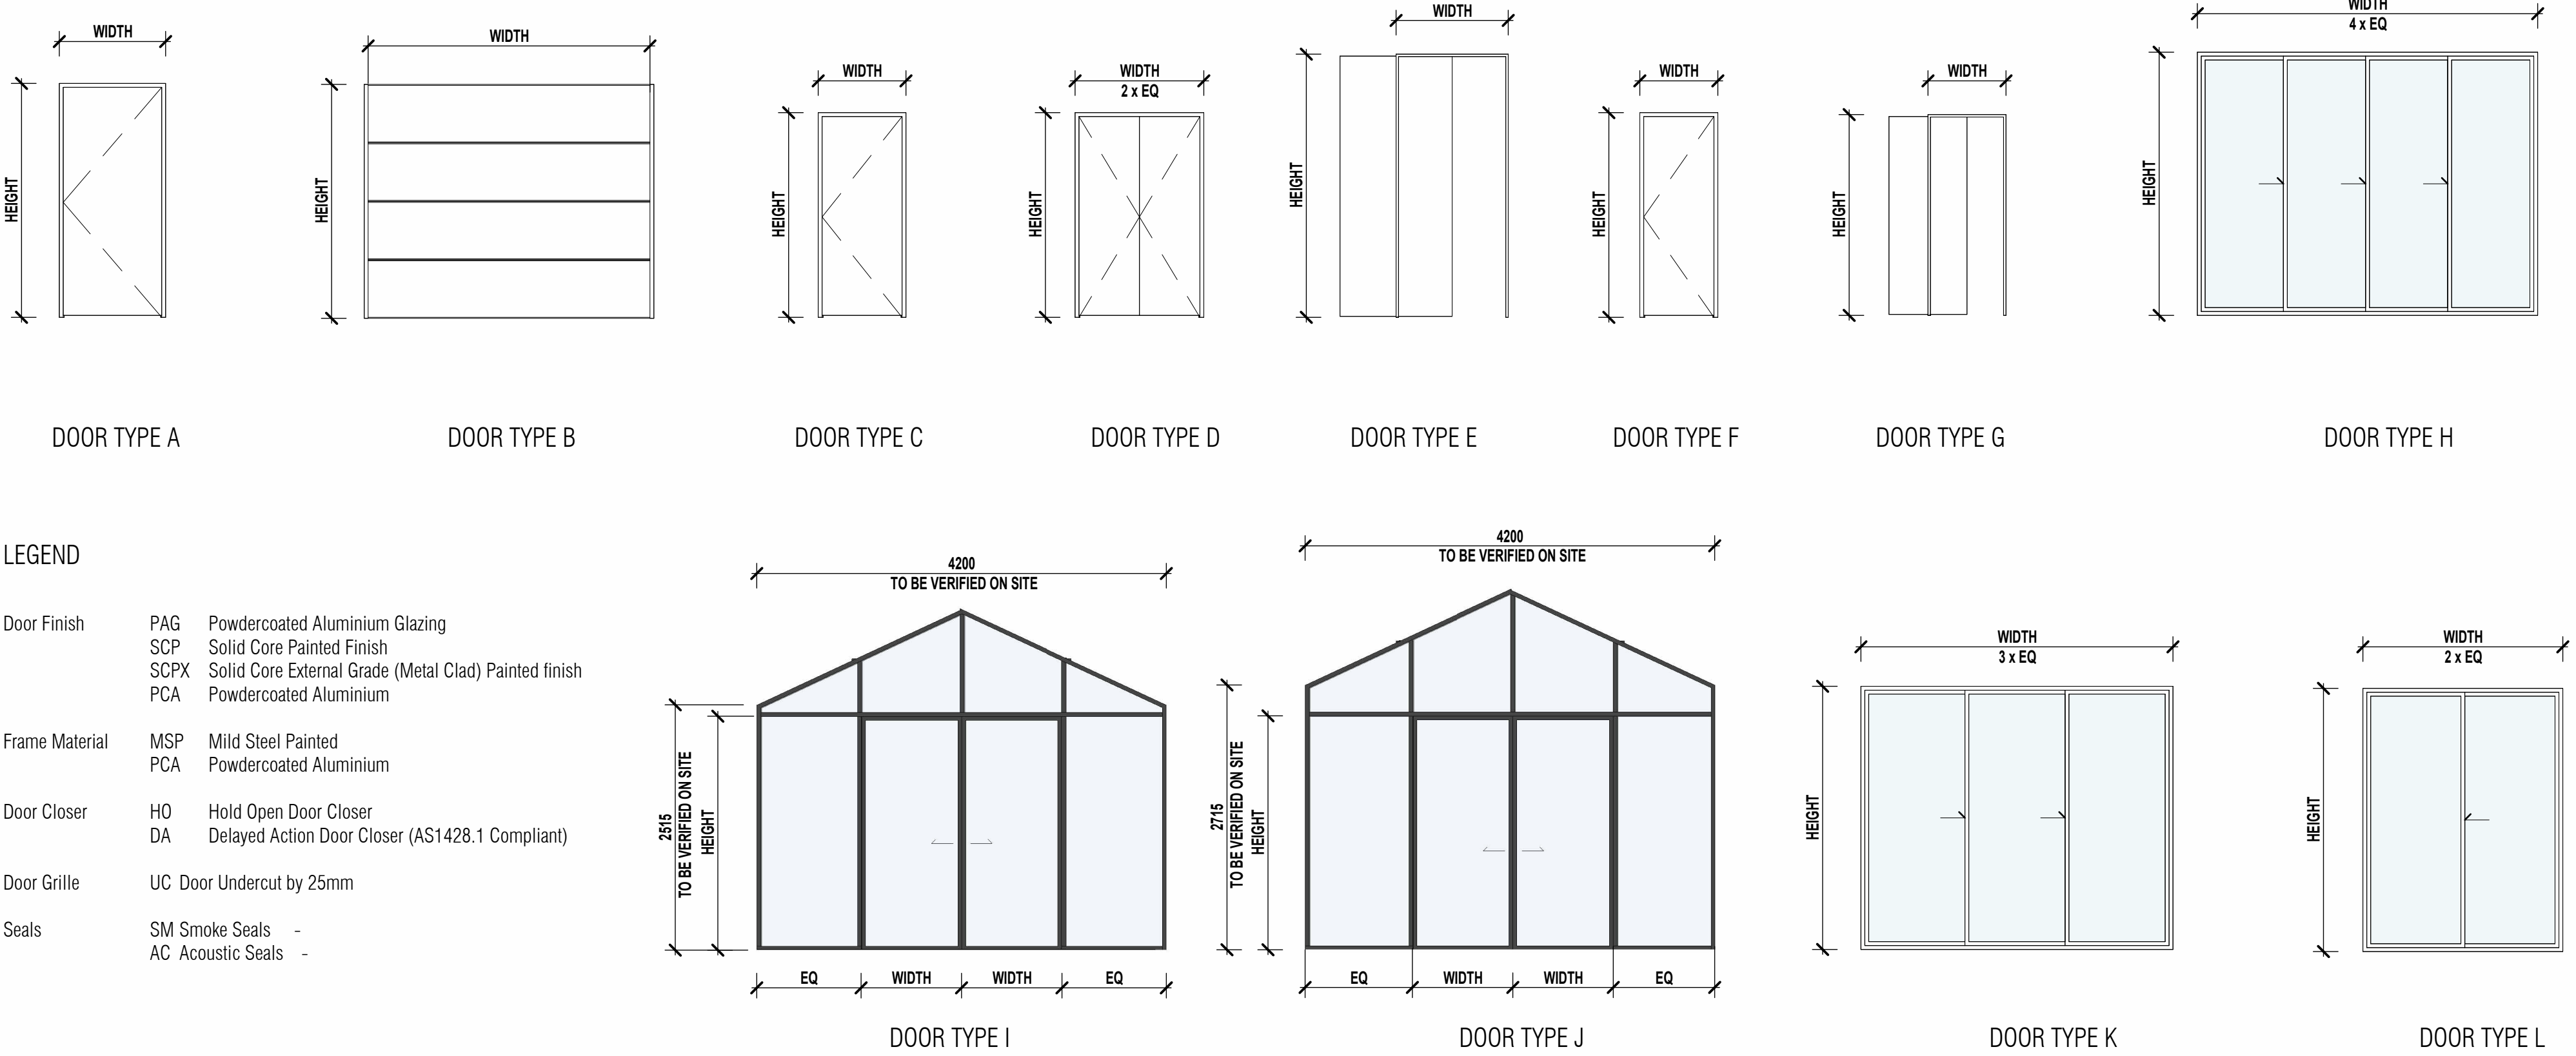

LEGEND

Door Finish	PAG	Powdercoated Aluminium Glazing
	SCP	Solid Core Painted Finish
	SCPX	Solid Core External Grade (Metal Clad) Painted finish
	PCA	Powdercoated Aluminium
Frame Material	MSP	Mild Steel Painted
	PCA	Powdercoated Aluminium
Door Closer	H0	Hold Open Door Closer
	DA	Delayed Action Door Closer (AS1428.1 Compliant)
Door Grille	UC	Door Undercut by 25mm
Seals	SM	Smoke Seals -
	AC	Acoustic Seals -


WINDOW SCHEDULE					
Mark	Height	Width	Sill Height	Description	Comments
A1	4000	625	300	PCA	FOYER
A2	600	1210	1500	PCA	GARAGE (HIGHLIGHT WINDOW)
A3	600	1210	1500	PCA	GARAGE (HIGHLIGHT WINDOW)
A4	600	970	1800	PCA	BATHROOM (HIGHLIGHT WINDOW)
A5	1300	1690	1100	PCA	BED ROOM
A6	1300	1690	1100	PCA	DINING/LIVING
A6	1300	1690	1100	PCA	DINING/LIVING
A7	600	970	1800	PCA	BATHROOM (HIGHLIGHT WINDOW)
A8	1300	1450	1100	PCA	BED ROOM
A9	1300	1690	1100	PCA	BED ROOM
A10	600	970	1800	PCA	BATHROOM (HIGHLIGHT WINDOW)
A11	600	2410	1800	PCA	BED ROOM (HIGHLIGHT WINDOW)
A12	1370	710	1100	PCA	KITCHEN (UNIT 3A)
A12	600	2410	1800	PCA	FAMILY ROOM (HIGHLIGHT)
B1	4000	625	300	PCA	FOYER
B2	600	1210	1500	PCA	GARAGE (HIGHLIGHT WINDOW)
B3	600	1210	1500	PCA	GARAGE (HIGHLIGHT WINDOW)
B4	600	970	1800	PCA	BATHROOM (HIGHLIGHT WINDOW)
B5	1300	1690	1100	PCA	BED ROOM
B6	600	1210	900	PCA	KITCHEN (UNIT 3B)
B7	600	970	1800	PCA	BATHROOM (HIGHLIGHT WINDOW)
B8	1300	1690	1100	PCA	BED ROOM
B9	1300	1690	1100	PCA	BED ROOM
B10	600	610	1800	PCA	BATHROOM (HIGHLIGHT WINDOW)
B11	600	2410	1800	PCA	BEDROOM (HIGHLIGHT WINDOW)
B12	600	2410	1800	PCA	FAMILY ROOM (HIGHLIGHT)

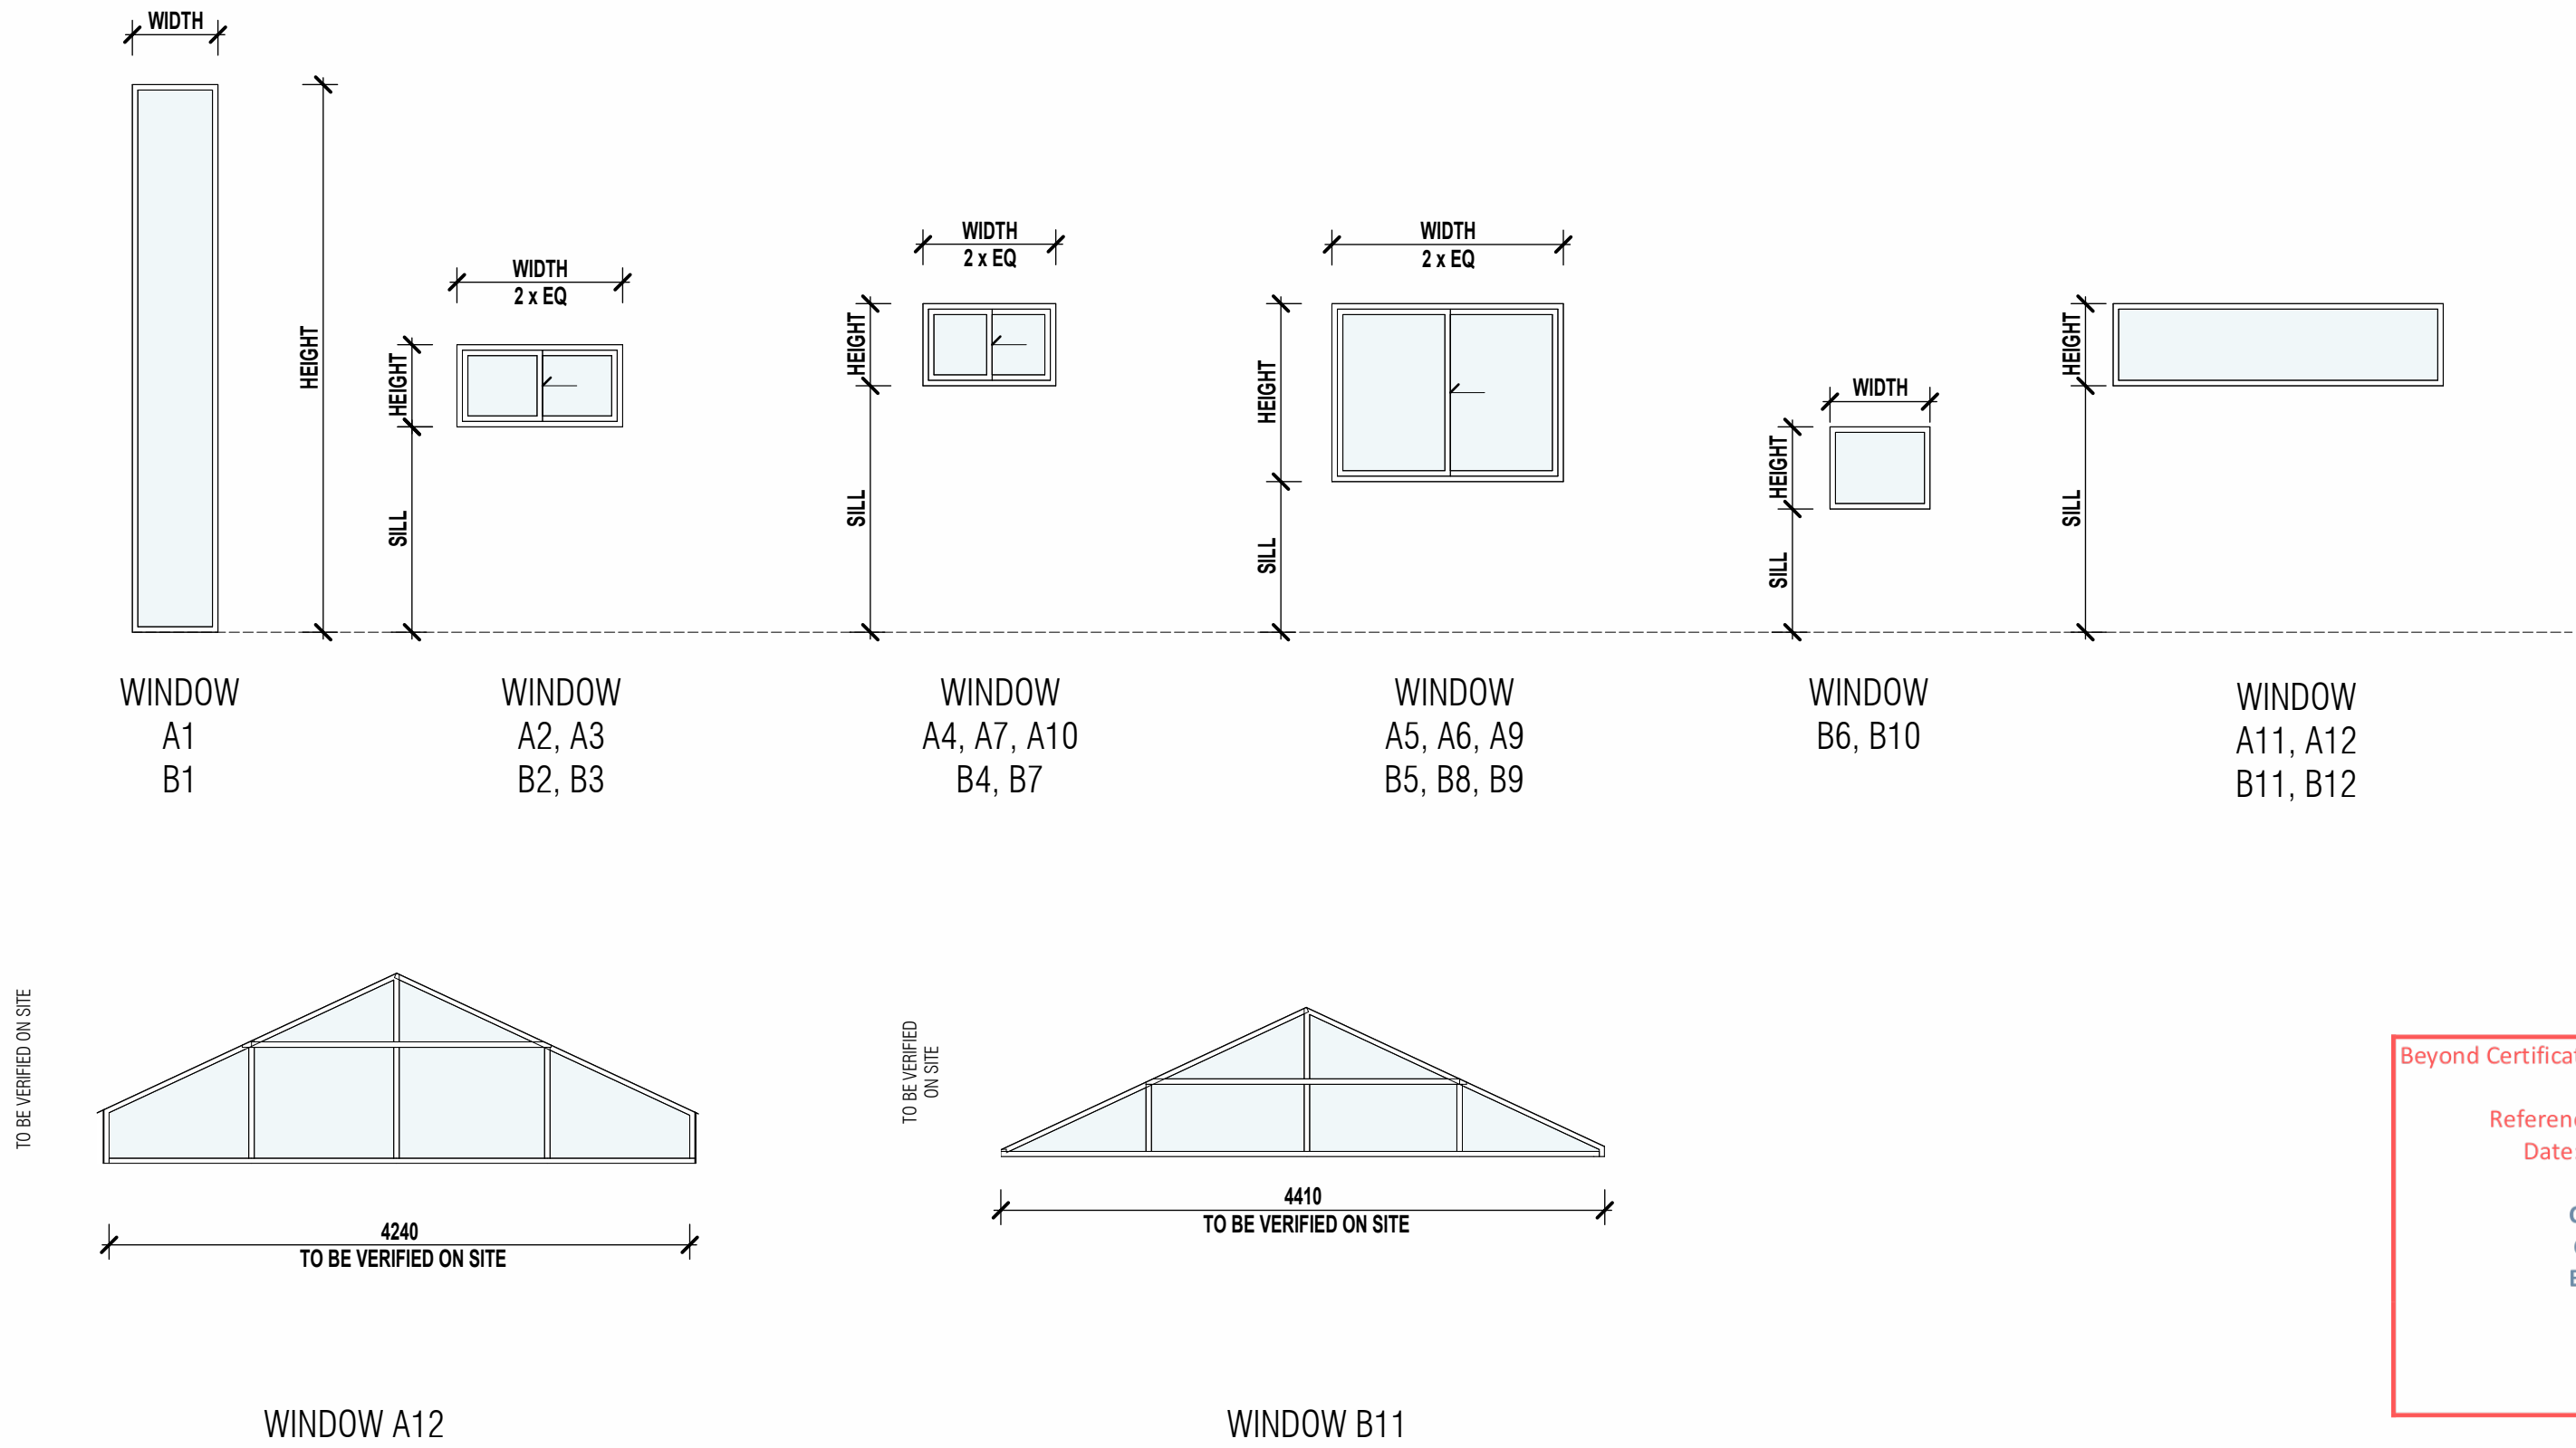

LEGEND		REMARKS
CLE	CLEAR GLAZING - EXTERNAL	1. ALUMINIUM COVER PLATE
OBS	OBSCURE GLAZING	TO MATCH WINDOWS
PCA	POWDER COATED ALUMINIUM	2. ELECTRICALLY OPERATED REMOTE CONTROLS
		3. MANUALLY OPERATED REMOTE CONTROLS

NOTE: ALL WINDOWS MUST BE SITE MEASURED BEFORE THE PREPARATION OF SHOP DRAWINGS & FABRICATION

REFER TO SECTION 'J' OF THE BCA FOR GLAZING VALUES

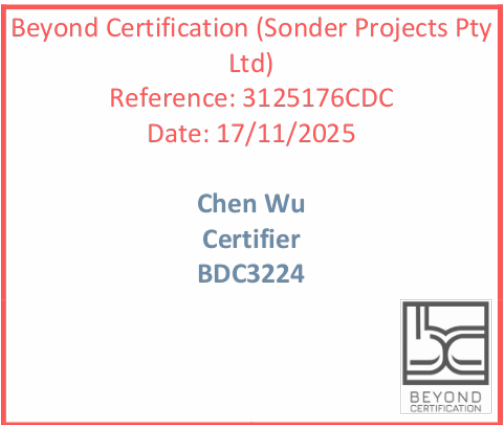

(iii) Thermal Performance and Materials				Show on DA plans	Show on CC/CDC plans & specs	Certifier check
(b) On a suspended floor, install insulation with an R-value of not less than 1.0 underneath the slab and around the vertical edges of the perimeter of the slab.						
(h) The applicant must construct the floors and walls of the development in accordance with the specifications listed in the table below.				✓	✓	✓
(i) The applicant must show on The plans accompanying The development application for The proposed development, The locations of ceiling fans set out in The Assessor Certificate.				✓		
(j) The applicant must show on the plans accompanying the application for a construction certificate (or complying development certificate, if applicable), the locations of ceiling fans set out in the Assessor Certificate.					✓	

Thermal loads			
Dwelling no.	Area adjusted heating load (in MJ/m ² /yr)	Area adjusted cooling load (in MJ/m ² /yr)	Area adjusted total load (in MJ/m ² /yr)
3A	16.1	13.1	29.20
All other dwellings	16.3	14.6	29.90

Construction of floors and walls				
Dwelling no.	Concrete slab on ground (m ²)	Suspended floor with open subfloor (m ²)	Suspended floor above enclosed subfloor (m ²)	Primarily rammed earth or mudbrick walls
3A	100.5	-	13	no
All other dwellings	100.8	-	13	no

Floor types										
Concrete slab on ground				Suspended floor above enclosed subfloor			Suspended floor above open subfloor			
Dwelling no.	Area (m ²)	Insulation	Low emissions option	Dematerialisation	Construction type	Area (m ²)	Insulation	Construction type	Area (m ²)	Insulation
3A	100.5	-	-	conventional slab	-	-	-	-	-	-
All other dwellings	100.8	-	-	conventional slab	-	-	-	-	-	-

BASIX Department of Planning, Housing and Infrastructure www.basix.nsw.gov.au Version: 4.03 / EUCALYPTUS_03_01_0 Certificate No.: 1809098M Tuesday, 19 August 2025 page 10/15

Floor types												
First floor above habitable rooms or mezzanine				Suspended floor above garage			Garage floor					
Dwelling no.	Construction type	Area (m ²)	Insulation	Construction type	Area (m ²)	Insulation	Construction type	Area (m ²)	Insulation	Low emissions option	Dematerialisation	
3A	concrete - suspended	92	-	concrete - suspended	13	-	concrete slab on ground	19	-	-	conventional slab	
All other dwellings	concrete - suspended	95	-	concrete - suspended	13	-	concrete slab on ground	19	-	-	conventional slab	
External walls												
External wall type 1				External wall type 2								
Dwelling no.	Wall type	Area (m ²)	Insulation	Low emissions option	Wall type	Area (m ²)	Insulation	Low emissions option	Wall type	Area (m ²)	Insulation	Low emissions option
3A	cavity brick	120	foil-foam composite board	none	brick veneer, frame - timber - H2 treated softwood	75	fibreglass batts or roll	none	brick veneer, frame - timber - H2 treated softwood	75	fibreglass batts or roll	none
All other dwellings	cavity brick	96	foil-foam composite board	none	brick veneer, frame - timber - H2 treated softwood	75	fibreglass batts or roll	none	brick veneer, frame - timber - H2 treated softwood	75	fibreglass batts or roll	none
External walls												
External wall type 3				External wall type 4								
Dwelling no.	Wall type	Area (m ²)	Insulation	Low emissions option	Wall type	Area (m ²)	Insulation	Low emissions option	Wall type	Area (m ²)	Insulation	Low emissions option
All dwellings	-	-	-	-	-	-	-	-	-	-	-	-

BASIX Department of Planning, Housing and Infrastructure www.basix.nsw.gov.au Version: 4.03 / EUCALYPTUS_03_01_0 Certificate No.: 1809098M Tuesday, 19 August 2025 page 10/15

Internal walls								
Internal walls shared with garage			Internal wall type 1			Internal wall type 2		
Dwelling no.	Wall type	Area (m ²)	Insulation	Wall type	Area (m ²)	Insulation	Wall type	Area (m ²)
All dwellings	plasterboard, frame - timber - H2 treated softwood	16.5	-	plasterboard, frame - timber - H2 treated softwood	135	-	-	-
Ceiling and roof								
Flat ceiling / pitched roof			Raked ceiling / pitched or skillion roof			Flat ceiling / flat roof		
Dwelling no.	Construction type	Area (m ²)	Insulation	Construction type	Area (m ²)	Insulation	Construction type	Area (m ²)
All dwellings	-	-	Ceiling-Roof	-	-	Ceiling-Roof	framed - metal roof, frame - timber - H2 treated softwood	140
Glazing type								
Dwelling no.	Single glazing (m ²)	Double glazing (m ²)	Triple glazing (m ²)	Aluminium frames (m ²)	Timber frames (m ²)	uPVC frames (m ²)	Steel frames (m ²)	Composite frames (m ²)
3A	46	-	-	46	-	-	-	-
All other dwellings	45	-	-	45	-	-	-	-

BASIX Department of Planning, Housing and Infrastructure www.basix.nsw.gov.au Version: 4.03 / EUCALYPTUS_03_01_0 Certificate No.: 1809098M Tuesday, 19 August 2025 page 10/15

2. Commitments for common areas and central systems/facilities for the development (non-building specific)				
(b) Common areas and central systems/facilities				
(i) Water	Show on DA plans	Show on CC/CDC plans & specs	Certifier check	
(a) If, in carrying out the development, the applicant installs a showerhead, toilet, tap or clothes washer into a common area, then that item must meet the specifications listed for it in the table.		✓	✓	
(b) The applicant must install (or ensure that the development is serviced by) the alternative water supply system(s) specified in the "Central systems" column of the table below, in each case, the system must be sized, be configured, and be connected, as specified in the table.	✓	✓	✓	
(c) A swimming pool or spa listed in the table must not have a volume (in kLs) greater than that specified for the pool or spa in the table.	✓	✓	✓	
(d) A pool or spa listed in the table must have a cover or shading if specified for the pool or spa in the table.		✓	✓	
(e) The applicant must install each fire sprinkler system listed in the table so that the system is configured as specified in the table.		✓	✓	
(f) The applicant must ensure that the central cooling system for a cooling tower is configured as specified in the table.		✓	✓	
Common area				
Showerheads rating	Toilets rating	Taps rating	Clothes washers rating	
All common areas	no common facility	no common facility	no common facility	no common laundry facility
(ii) Energy				
Show on DA plans	Show on CC/CDC plans & specs	Certifier check		
(a) If, in carrying out the development, the applicant installs a ventilation system to service a common area specified in the table below, then that ventilation system must be of the type specified for that common area, and must meet the efficiency measure specified.	✓	✓	✓	
(b) In carrying out the development, the applicant must install, as the "primary type of artificial lighting" for each common area specified in the table below, the lighting specified for that common area. This lighting must meet the efficiency measure specified. The applicant must also install a centralised lighting control system or Building Management System (BMS) for the common area, where specified.		✓	✓	
(c) The applicant must install the systems and fixtures specified in the "Central energy systems" column of the table below. In each case, the system or fixture must be of the type, and meet the specifications, listed for it in the table.	✓	✓	✓	

BASIX Department of Planning, Housing and Infrastructure www.basix.nsw.gov.au Version: 4.03 / EUCALYPTUS_03_01_0 Certificate No.: 1809098M Tuesday, 19 August 2025 page 10/15

Central energy systems	Type	Specification
Other	-	-

BASIX Department of Planning, Housing and Infrastructure www.basix.nsw.gov.au Version: 4.03 / EUCALYPTUS_03_01_0 Certificate No.: 1809098M Tuesday, 19 August 2025 page 10/15

Notes	
1. In these commitments, "applicant" means the person carrying out the development.	
2. The applicant must identify each dwelling, building and common area listed in this certificate, on the plans accompanying any development application, and on the plans and specifications accompanying the application for a construction certificate / complying development certificate, for the proposed development, using the same identifying letter or reference as is given to that dwelling, building or common area in this certificate.	
3. This note applies if the proposed development involves the erection of a building for both residential and non-residential purposes (or the change of use of a building for both residential and non-residential purposes). Commitments in this certificate which are specified to apply to a "common area" of a building or the development, apply only to that part of the building or development to be used for residential purposes.	
4. If this certificate lists a central system as a commitment for a dwelling or building, and that system will also service any other dwelling or building within the development, then that system need only be installed once (even if it is separately listed as a commitment for that other dwelling or building).	
5. If a star or other rating is specified in a commitment, this is a minimum rating.	
6. All alternative water systems to be installed under these commitments (if any), must be installed in accordance with the requirements of all applicable regulatory authorities. NOTE: NSW Health does not recommend that stormwater, recycled water or private dam water be used to irrigate edible plants which are consumed raw, or that rainwater be used for human consumption in areas with potable water supply.	
Legend	
1. Commitments identified with a "✓" in the "Show on DA plans" column must be shown on the plans accompanying the development application for the proposed development (if a development application is to be lodged for the proposed development).	
2. Commitments identified with a "✓" in the "Show on CC/CDC plans and specs" column must be shown in the plans and specifications accompanying the application for a construction certificate / complying development certificate for the proposed development.	
3. Commitments identified with a "✓" in the "Certifier check" column must be certified by a certifying authority as having been fulfilled. (Note: a certifying authority must not issue an occupation certificate (either interim or final) for a building listed in this certificate, or for any part of such a building, unless it is satisfied that each of the commitments whose fulfillment it is required to monitor in relation to the building or part, has been fulfilled).	

BASIX Department of Planning, Housing and Infrastructure www.basix.nsw.gov.au Version: 4.03 / EUCALYPTUS_03_01_0 Certificate No.: 1809098M Tuesday, 19 August 2025 page 10/15

Nationwide House Energy Rating Scheme®

Multiple Class 1 Dwellings Summary

NatHERS® Certificate No. A2VVDU9KIE

Generated on 18 Aug 2025 using FirstRate5 v5.5.5a

Property

Address

Lot/DP

NatHERS Climate Zone

2/-/DP31795, 3 Johnston Avenue, Kirrawee, NSW, 2232

Mascot (Sydney Airport)

Accredited assessor

Name

Business name

Email

Phone

Accreditation No.

Assessor Accrediting Organisation

Stephen Burgum

V-Star Energy in association with Ecoplus Consultants

info@vstarenergy.com.au

0421810026

DMN/18/1890

NATIONWIDE HOUSE ENERGY RATING SCHEME®

To verify this certificate, scan the QR code or visit <https://www.fr5.com.au/QRCodeLanding?PublicId=A2VVDU9KIE&GrpCert=1>

When using either link, ensure you are visiting www.fr5.com.au.

National Construction Code (NCC) requirements

The NCC allows the use of NatHERS accredited software to comply with the energy efficiency requirements for houses (Class 1 buildings) and apartments (Class 2 sole-occupancy units and Class 4 parts of buildings). The applicable requirements for houses are detailed in Specification 42 of NCC Volume Two. For apartments the requirements are detailed in clauses J3D3 and J3D15 of NCC Volume One.

NCC 2022 includes enhanced thermal performance requirements for houses and apartments. It also includes a new whole-of-home annual energy use budget which applies to the major equipment in the home.

The NCC, and associated ABCB Standards and support material, can be accessed at www.abcb.gov.au.

Note, variations and additions to the NCC energy efficiency requirements may apply in some states and territories.

Summary of all dwellings

Certificate number and link	Unit number	Heating load (load limit) [MJ/m ² /p.a.]	Cooling load (load limit) [MJ/m ² /p.a.]	Total load [MJ/m ² /p.a.]	Star rating	Whole of Home Rating
YH159QRTOG		14.9 (N/A)	14.9 (N/A)	29.8	7	NA
UTENIKMJO		12.4 (N/A)	14.1 (N/A)	26.5	7.4	NA

Nationwide House Energy Rating Scheme (NatHERS) is an initiative of the Australian, state and territory governments. For more details see www.nathers.gov.au.

Generated on 18 Aug 2025 using FirstRate5 v5.5.5a for 2/-/DP31795, 3 Johnston Avenue, Kirrawee, NSW, 2232

Page 1 of 2

COPYRIGHT & GENERAL NOTE:
Figured dimensions shall be taken in preference to scaling. Drawing to be read in conjunction with information on first page. Check all dimensions and levels on site before commencing work or ordering materials. All existing ground lines & trees location are approximate, therefore, to be verified on-site by the builder. Any discrepancies to be verified back to Zhin Architects before proceeding. All workmanship and materials shall comply with all relevant codes, ordinances, Australian Standards and manufacturers' instructions. Unless noted issued for Constructor (drawing not to be used for construction). All art / graphic representations are indicative only. Information on this drawing is the copyright of Zhin Architects. Copying or using this drawing in whole or part without written permission infringes copyright.

C	ISSUE FOR CDC SUBMISSION 3	7/11/2025	TH	IC
B	ISSUE FOR CDC SUBMISSION 2	28/02/2025	TH	IC
A	ISSUE FOR CDC SUBMISSION	18/09/2025	TH	IC
ISSUE	AMENDMENT	DATE	DRAWN	CHECK

Drawing is NOT VALID or issued for use, unless checked

PROJECT ARCHITECTS
IAN CONRY

REGISTRATION NUMBER
NSW No. 8317

Zhin Architects Pty Ltd

+61 2 8893 8888
info@zhinarch.com.au
www.zhinarch.com.au
28 495 869 790 / abn

PROJECT STATUS:
Complying Development Certificate

PROJECT NAME
Dual Occupancy

3 Johnston Ave
Kirrawee, NSW 2232
LGA: SUTHERLAND SHIRE COUNCIL

Checked
Checker
8848
JOB No.

CDC 501
DRAWING No.

scale 1:100 @A1sheet


7/11/2025 12:59 PM

COPYRIGHT & GENERAL NOTE:
Figured dimensions shall be taken in preference to scaling. Drawing to be read in conjunction with information on first page. Check all dimensions and levels on site before commencing work or ordering materials. All existing ground lines & trees location are approximate, therefore, to be verified on-site by the builder. Any discrepancies to be verified back to Zhin Architects before proceeding. All workmanship and materials shall comply with all relevant codes, ordinances, Australian Standards and manufacturers' instructions. Unless noted issued for Constructor (drawing not to be used for construction). All art / graphic representations are indicative only. Information on this drawing is the copyright of Zhin Architects. Copying or using this drawing in whole or part without written permission infringes copyright.


7/11/2025 12:59 PM

SCALE @A1 SHEET
1 : 15


C
ISSUE

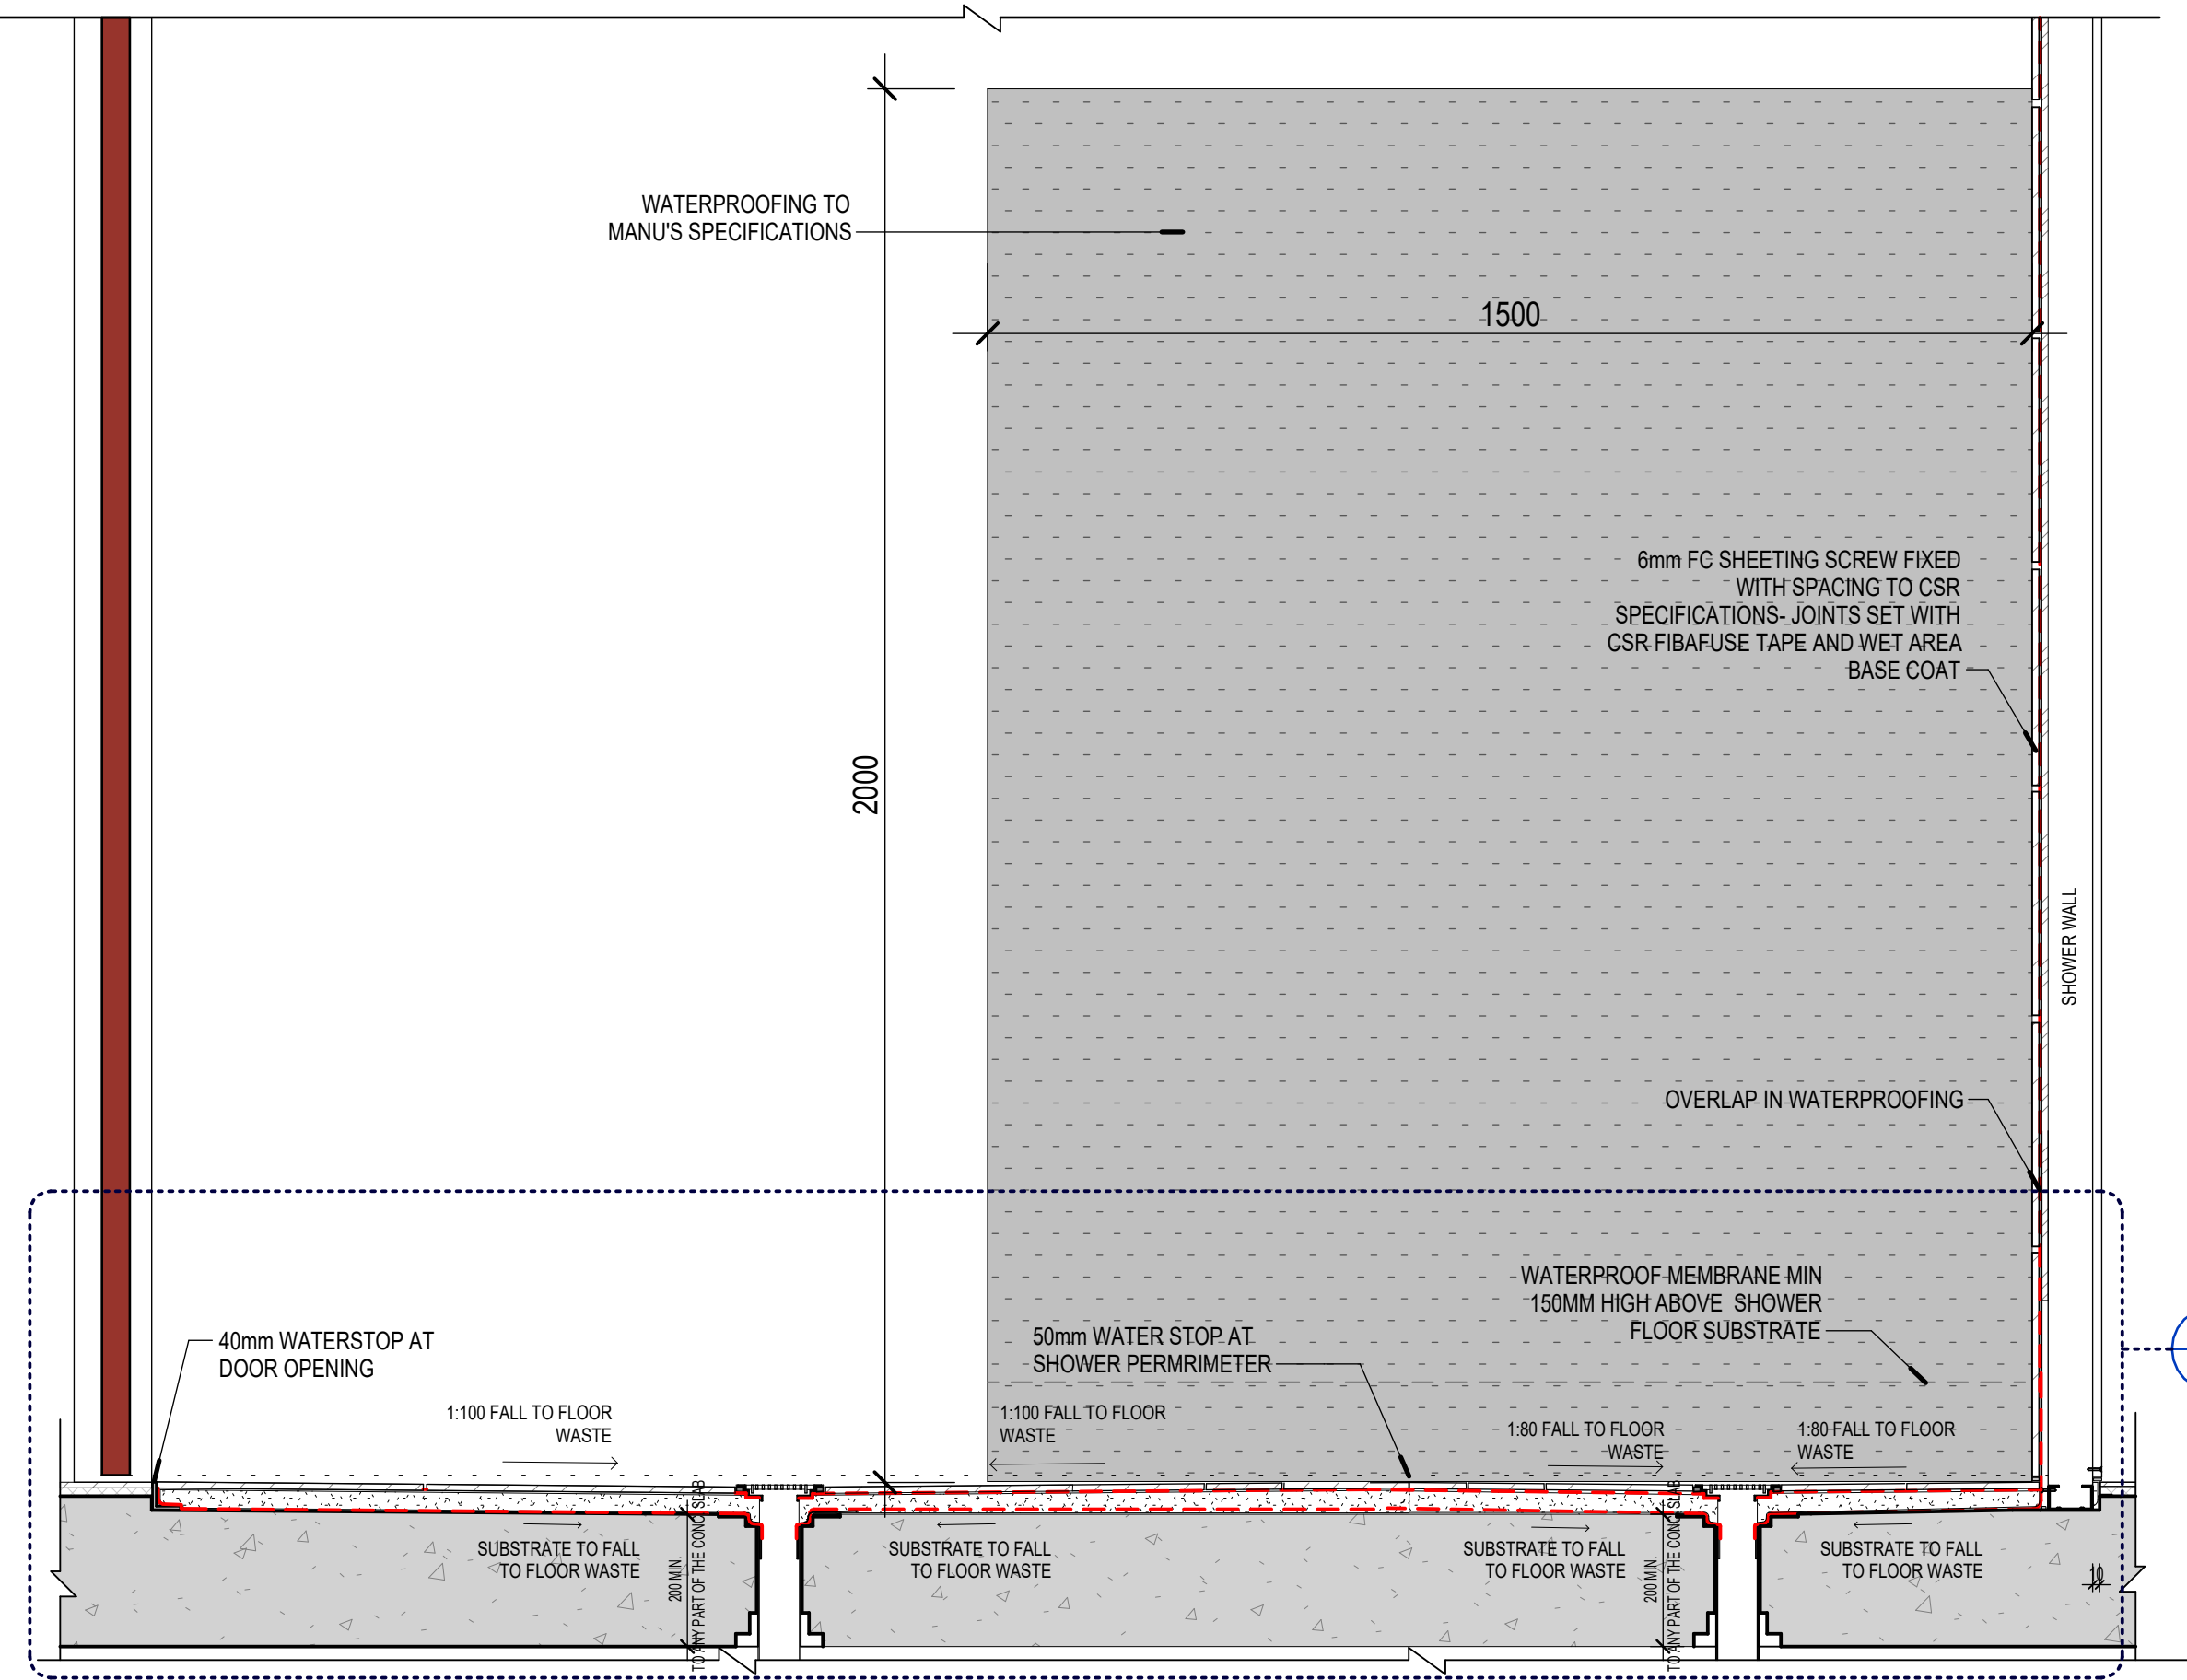


2 ENCLOSED SHOWER - SIDE VIEW 1
1: 10

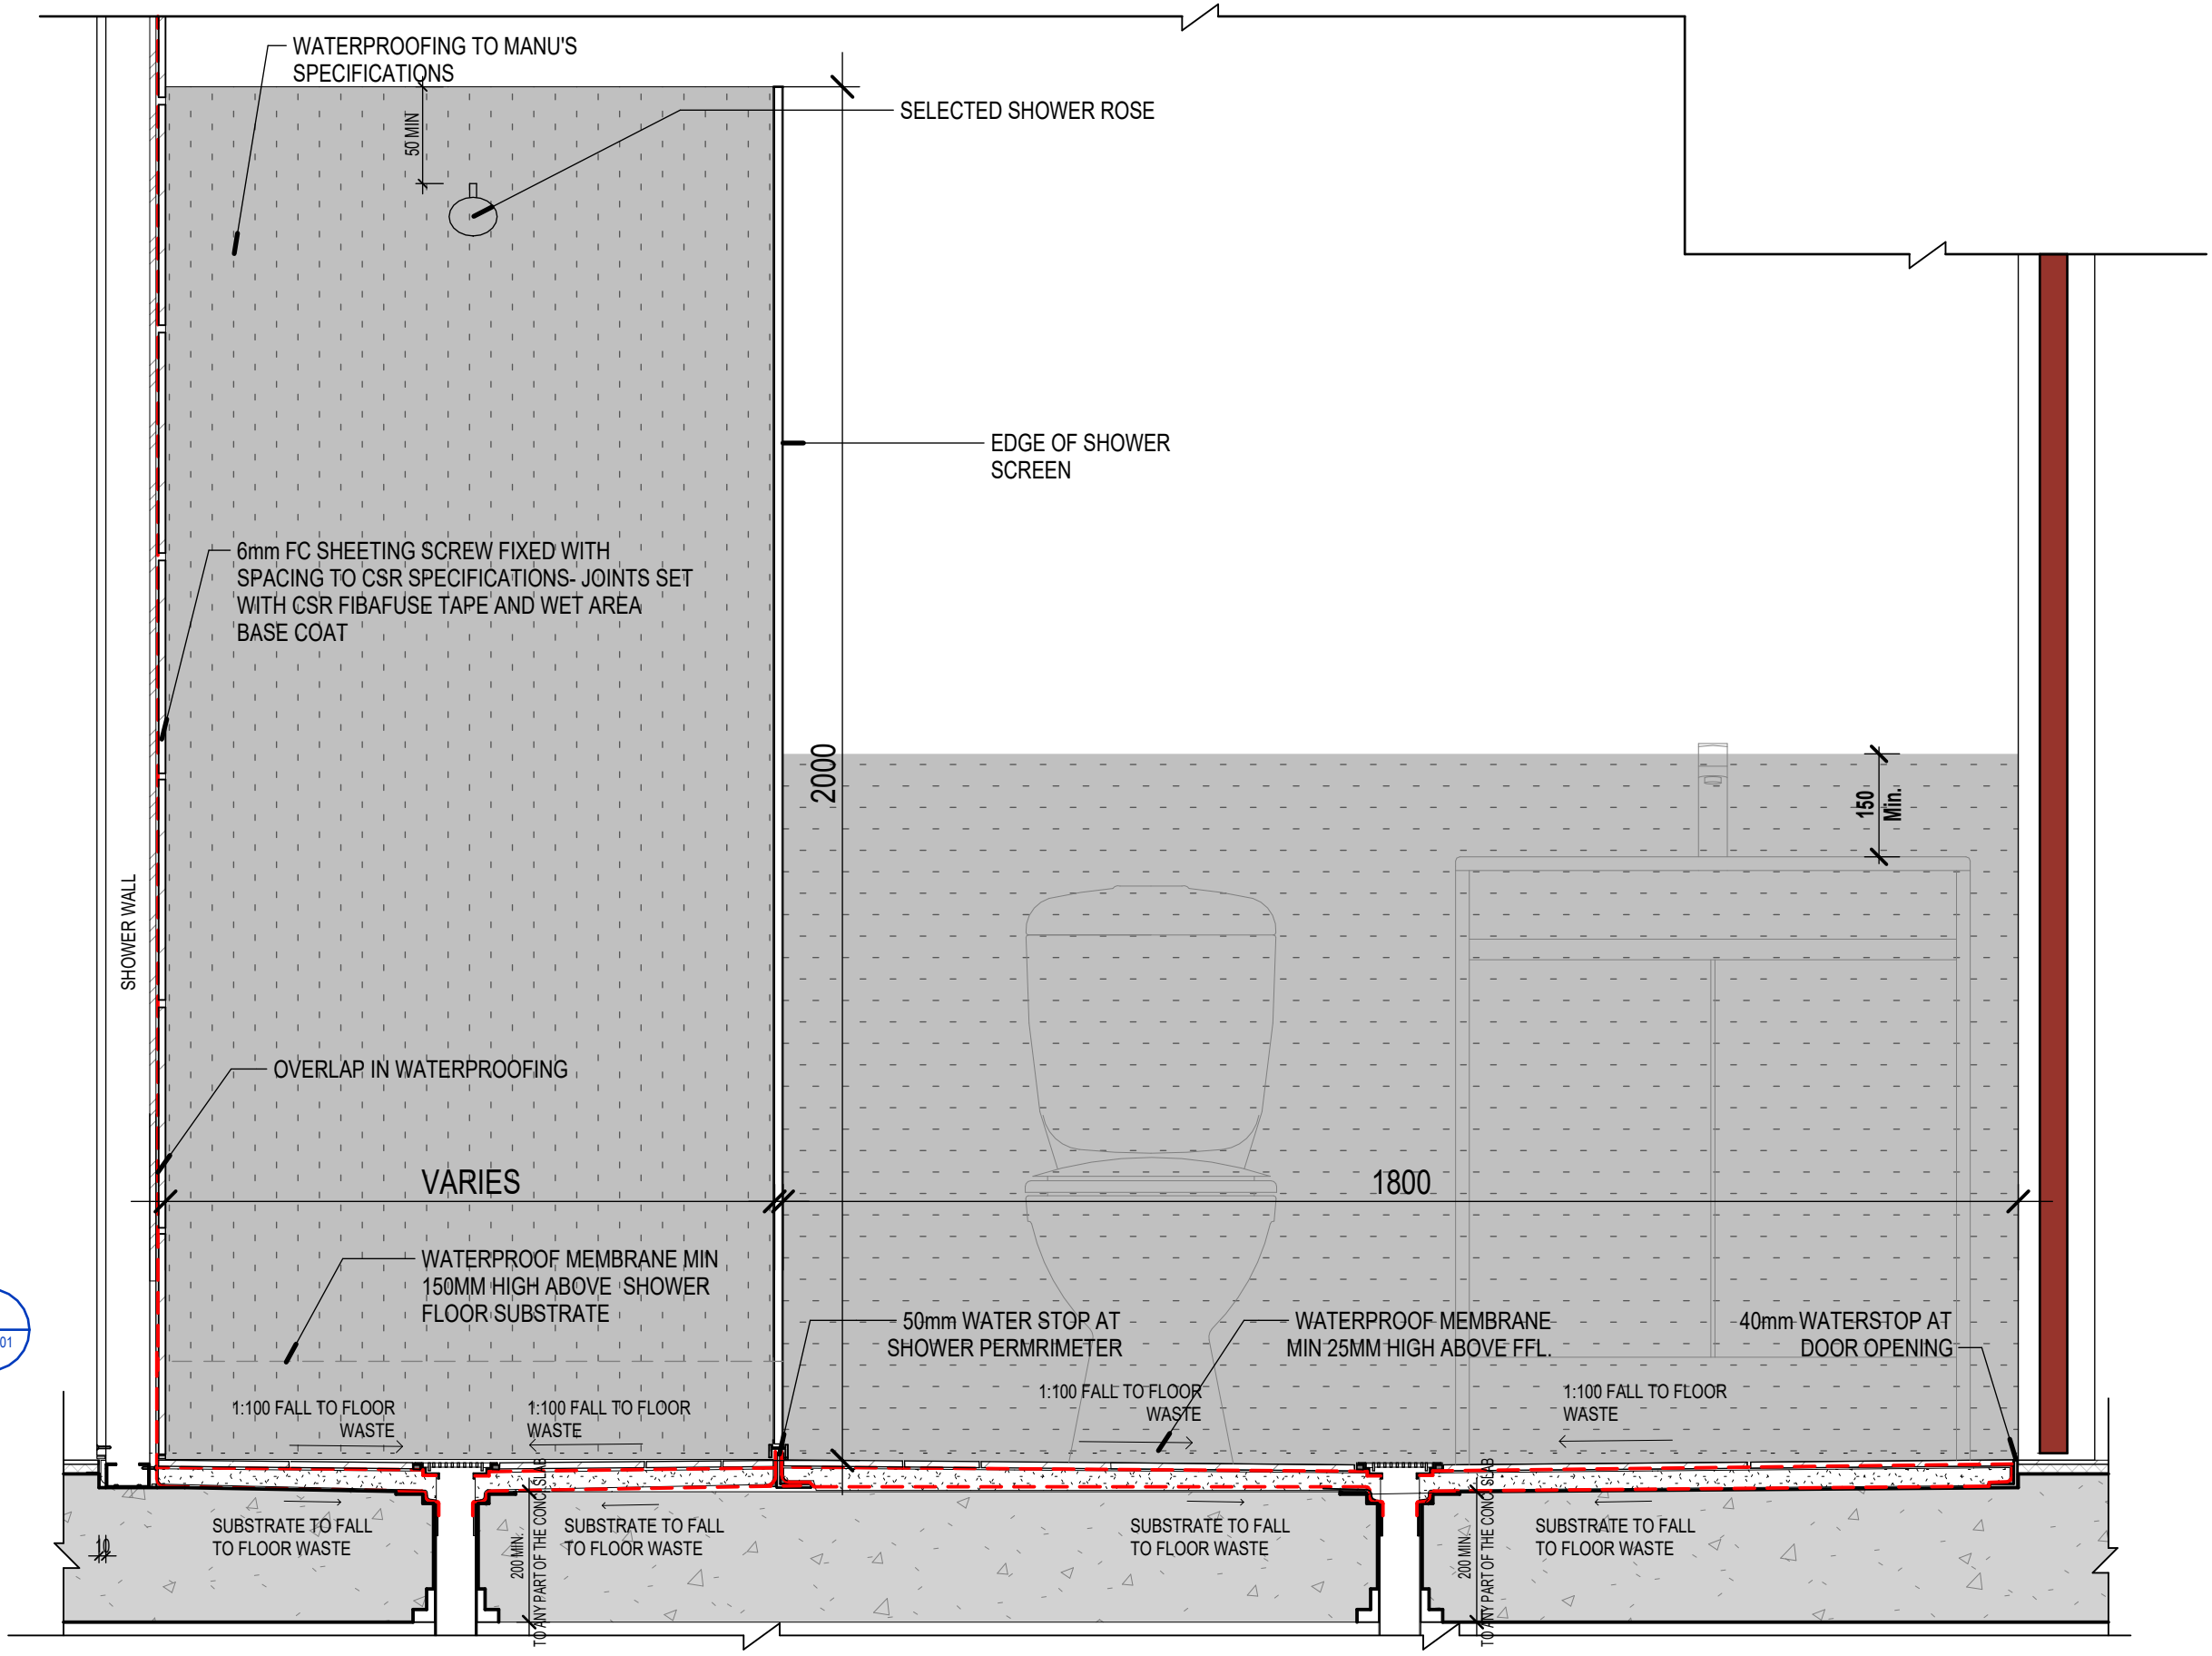


4 ENCLOSED SHOWER - SIDE VIEW 2
1: 10

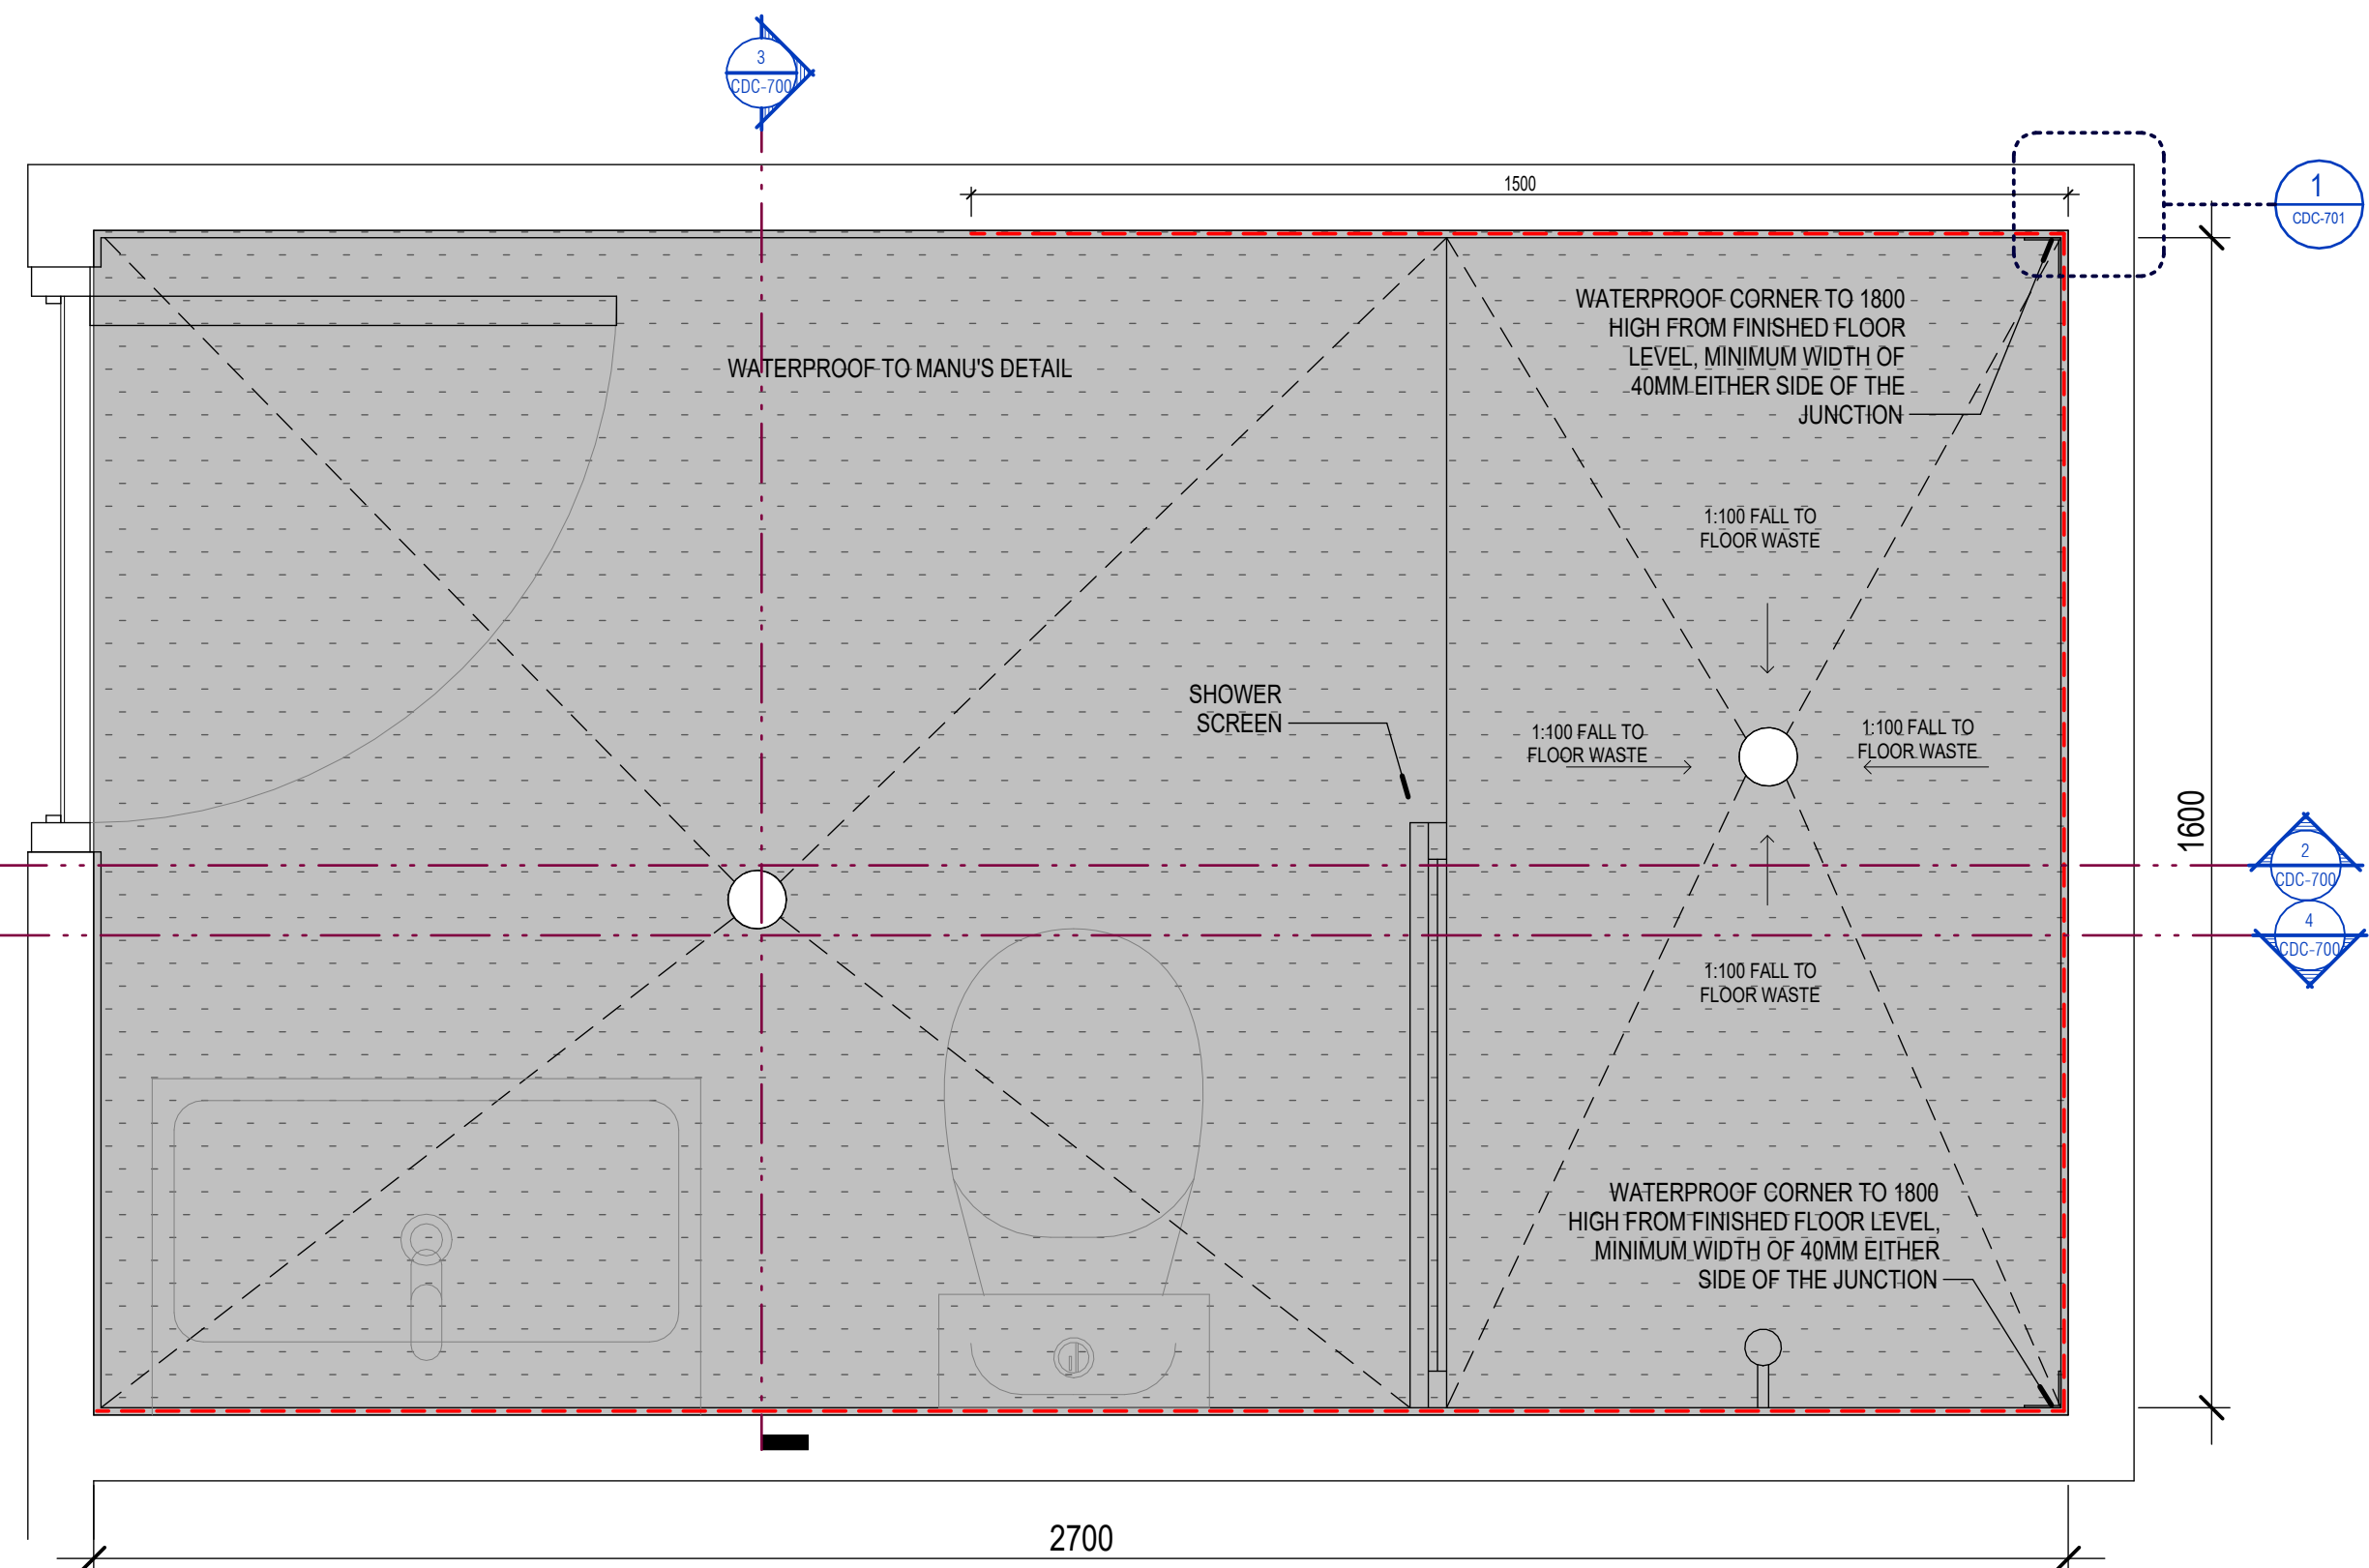

1 TYPICAL ENCLOSED SHOWER - PLAN VIEW
1: 10

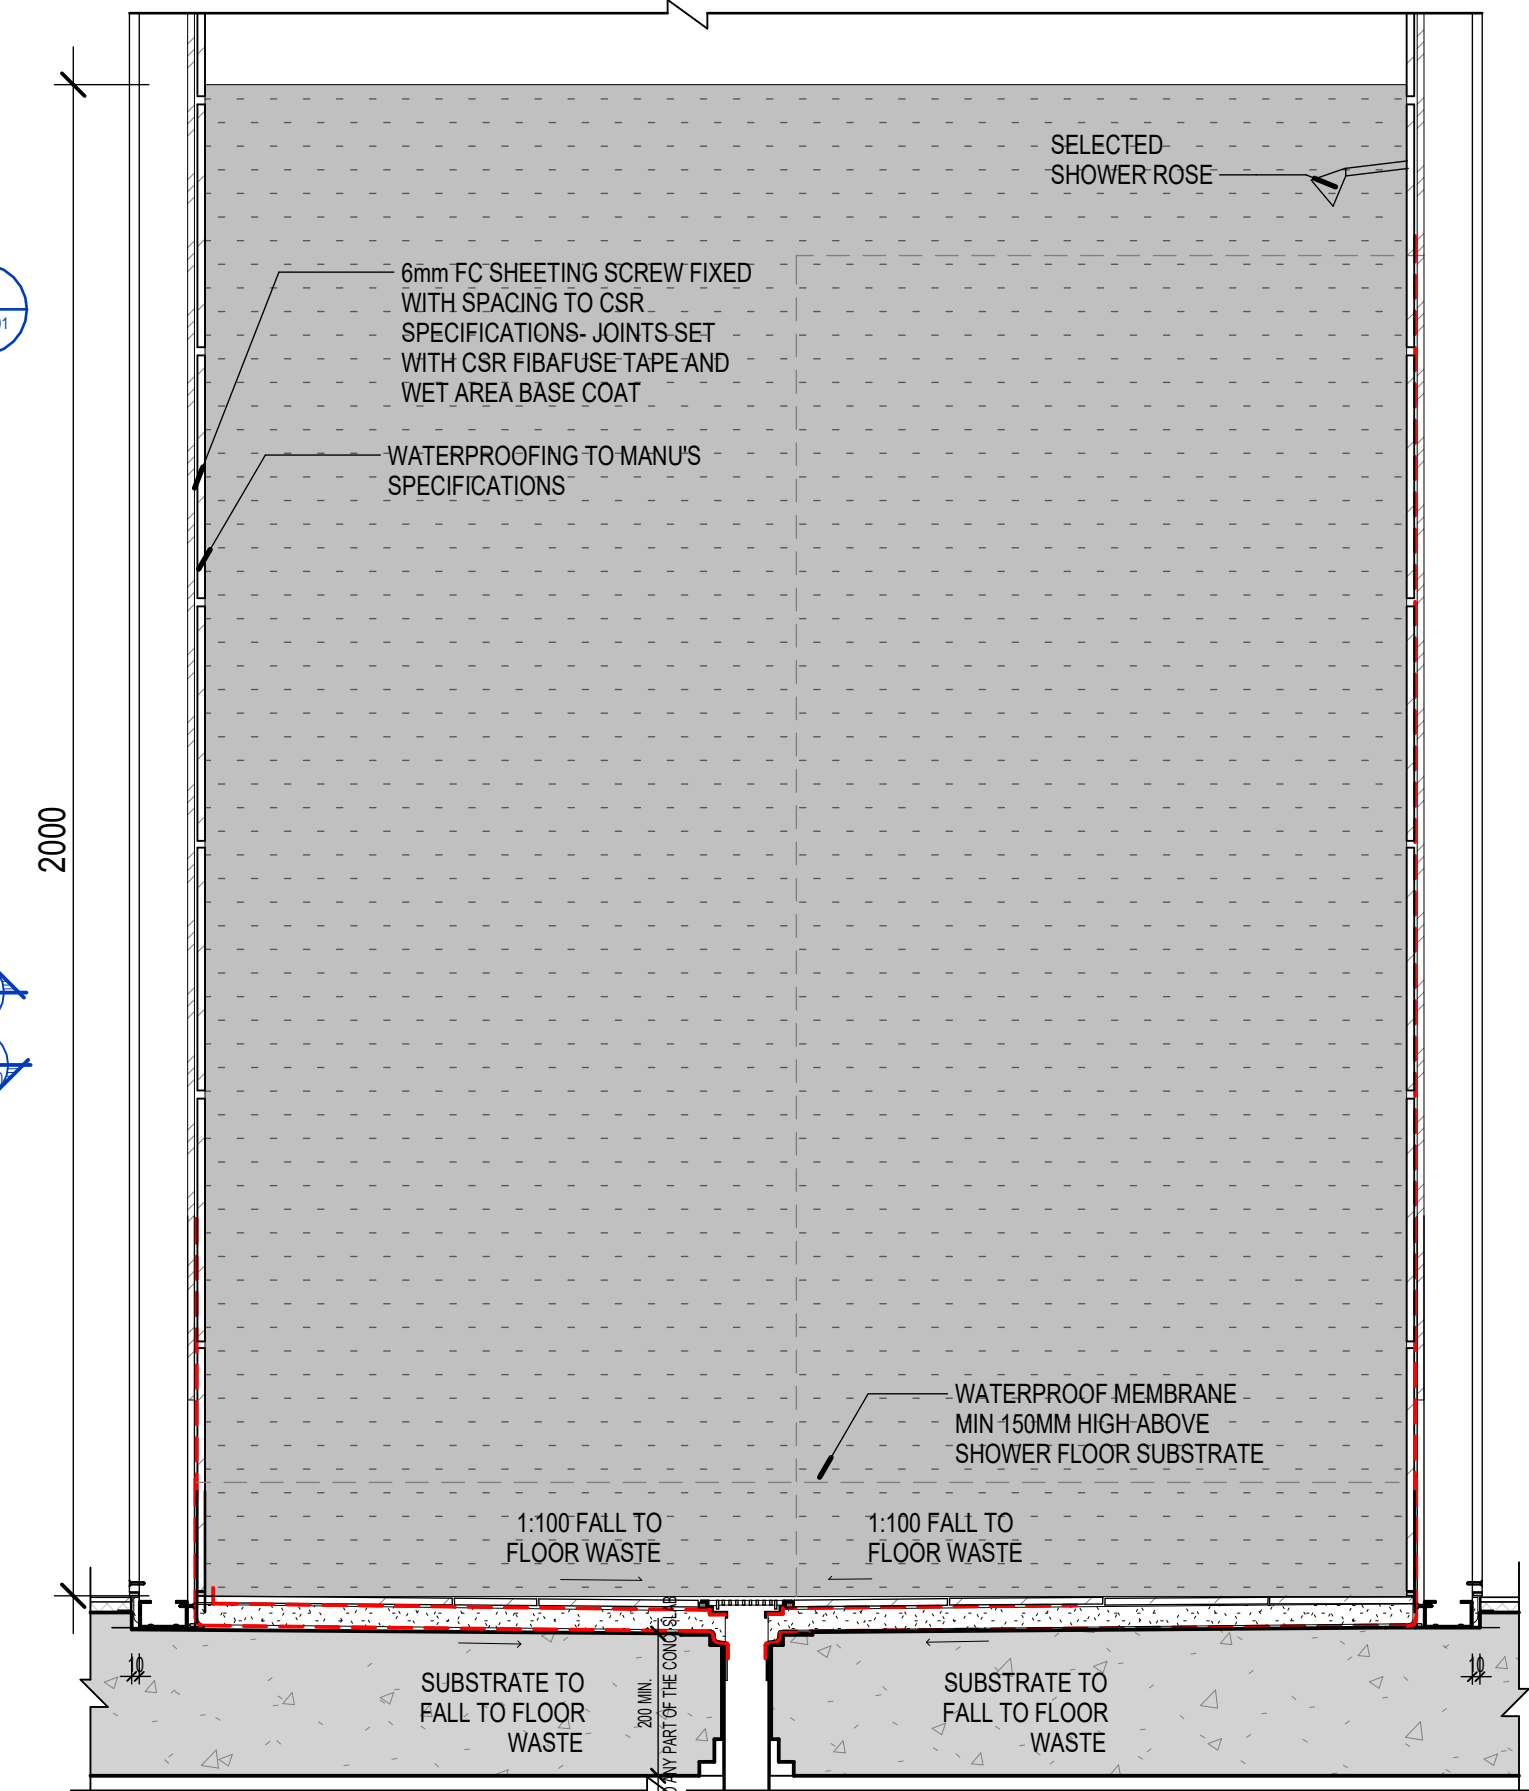

3 ENCLOSED SHOWER - FRONT VIEW
1: 10

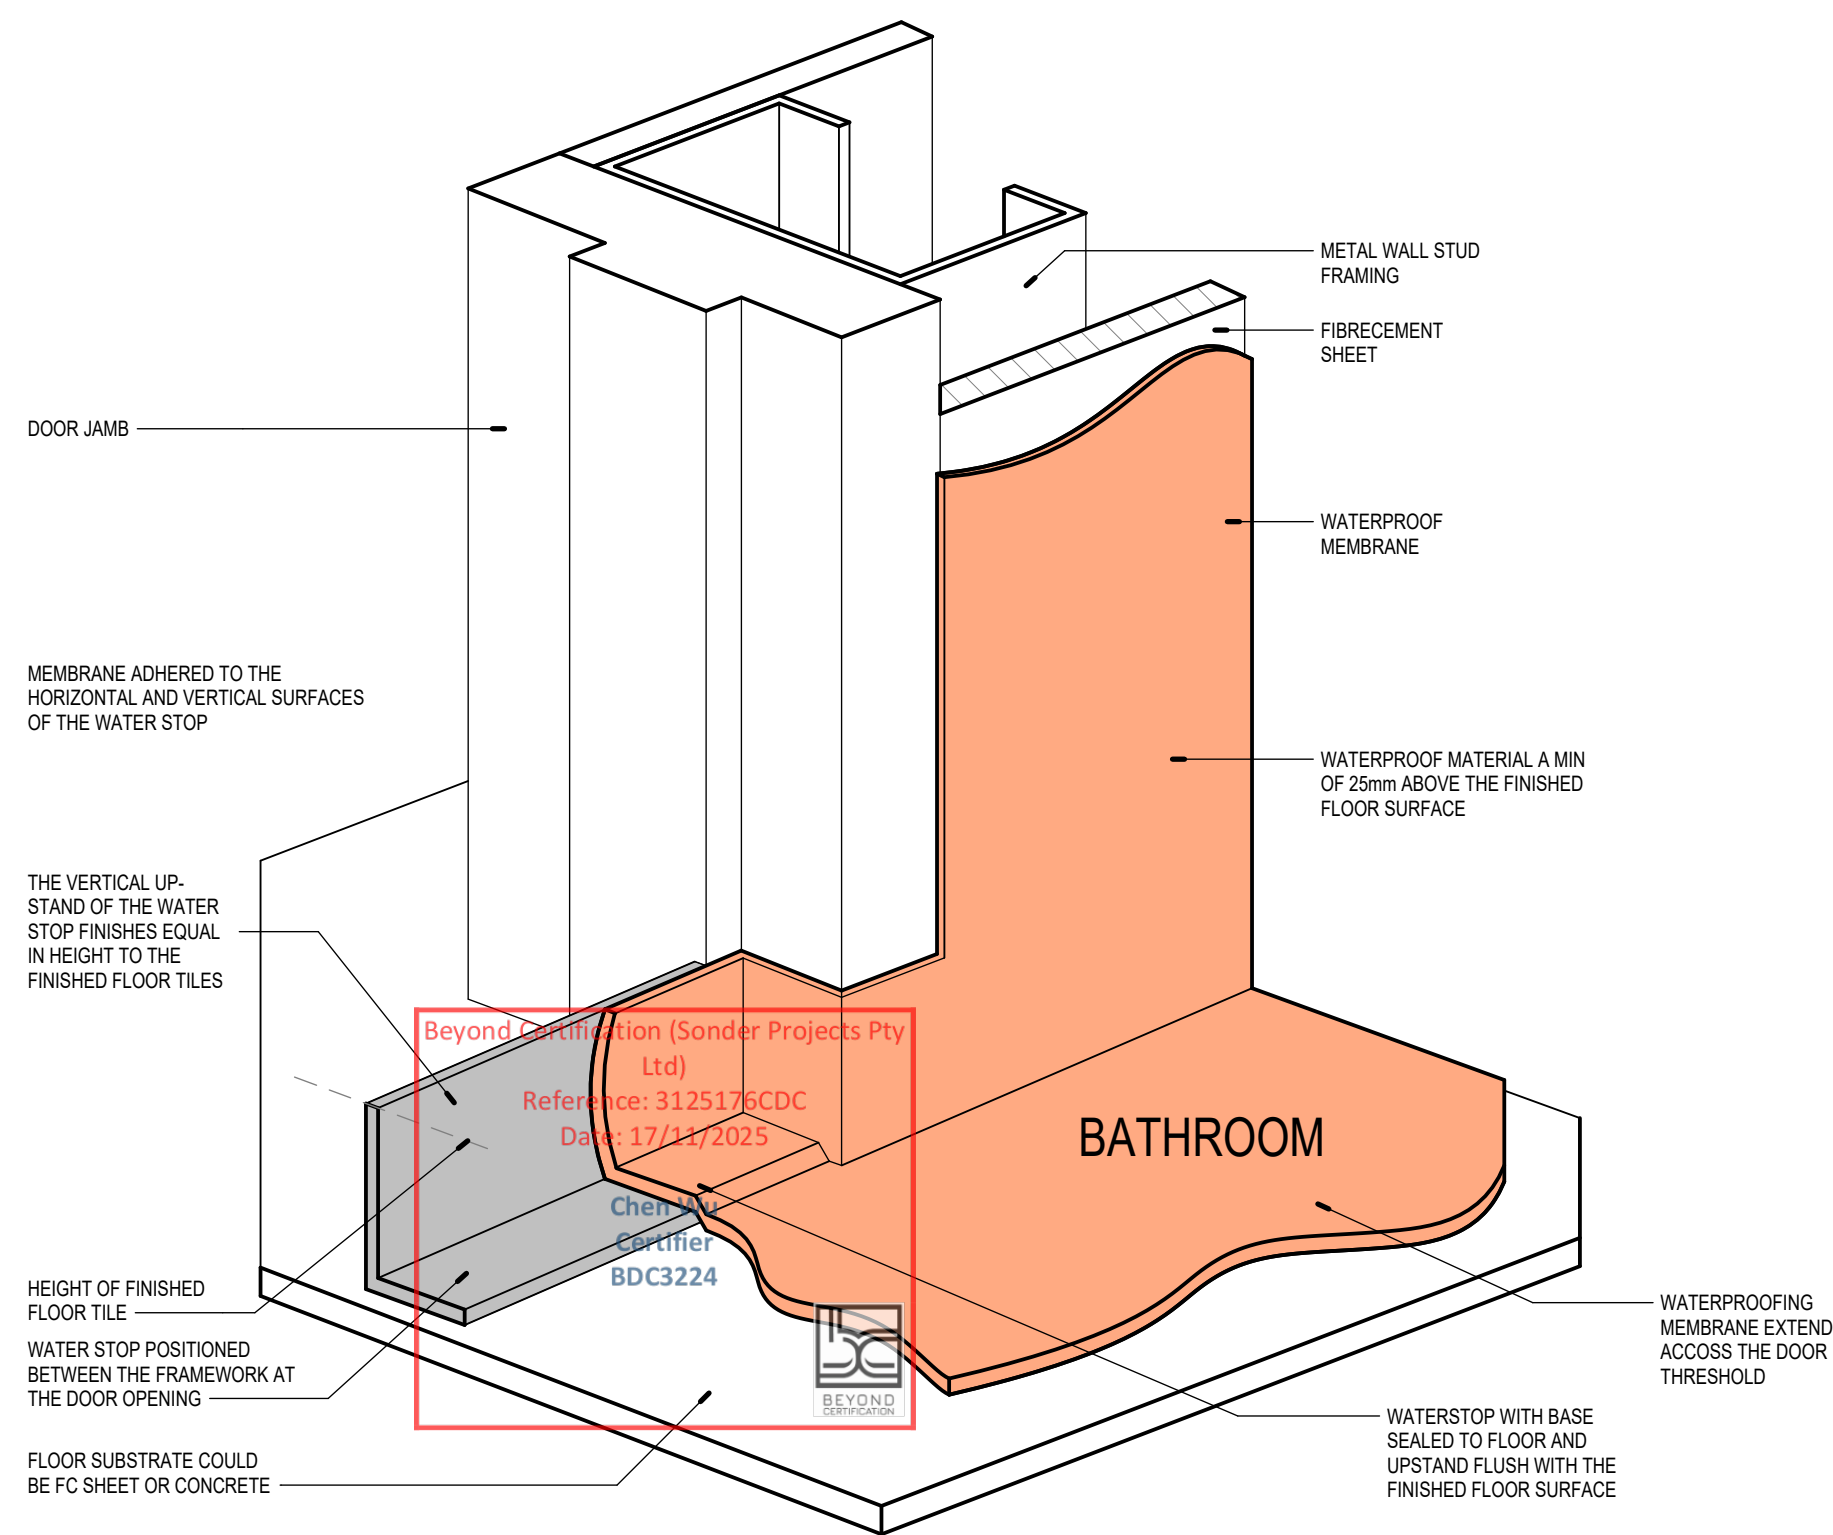

5 WATER STOP AT DOOR THRESHOLD - SHEET MEMBRANE
1: 1

COPYRIGHT & GENERAL NOTE:
Figured dimensions shall be taken in preference to scaling. Drawing to be read in conjunction with information on first page. Check all dimensions and levels on site before commencing work or ordering materials. All existing ground lines & levels location are approximate, therefore, to be verified on-site by the builder. Any discrepancies to be verified back to Zhihar Architects before proceeding. All workmanship and materials shall comply with all relevant codes, ordinances, Australian Standards and manufacturers' instructions. Unless noted issued for Construction Drawing not to be used for construction. All art / graphic representations are indicative only. Information on this drawing is the copyright of Zhihar Architects. Copying or using this drawing in whole or part without written permission infringes copyright.

C	ISSUE FOR CDC SUBMISSION 3	7/11/2025	TH	IC
B	ISSUE FOR CDC SUBMISSION 2	28/10/2025	TH	IC
A	ISSUE FOR CDC SUBMISSION	18/09/2025	TH	IC
ISSUE	AMENDMENT	DATE	DRAWN	CHECK

Drawing is NOT VALID or issued for use, unless checked

PROJECT ARCHITECTS
IAN CONRY



REGISTRATION NUMBER
NSW No. 8317



Zhihar Architects Pty Ltd
Suite 1, Level 2
2 Rowe Street
Eastwood, NSW 2122
~61 2 8893 8888 / o
info@zhihar.com.au / o
www.zhihar.com.au / w
28 495 869 790 / abn

PROJECT STATUS:
Complying Development Certificate

PROJECT NAME
Dual Occupancy

3 Johnston Ave
Kirrawee, NSW 2232
L.G.A.: SUTHERLAND SHIRE COUNCIL









SHEET TITLE
WET AREA DETAILS 1

Checked
Checker
8848
JOB No.

CDC-700
DRAWING No.

SCALE @A1 SHEET
As indicated
C
ISSUE

scale 1:100 @A1 sheet

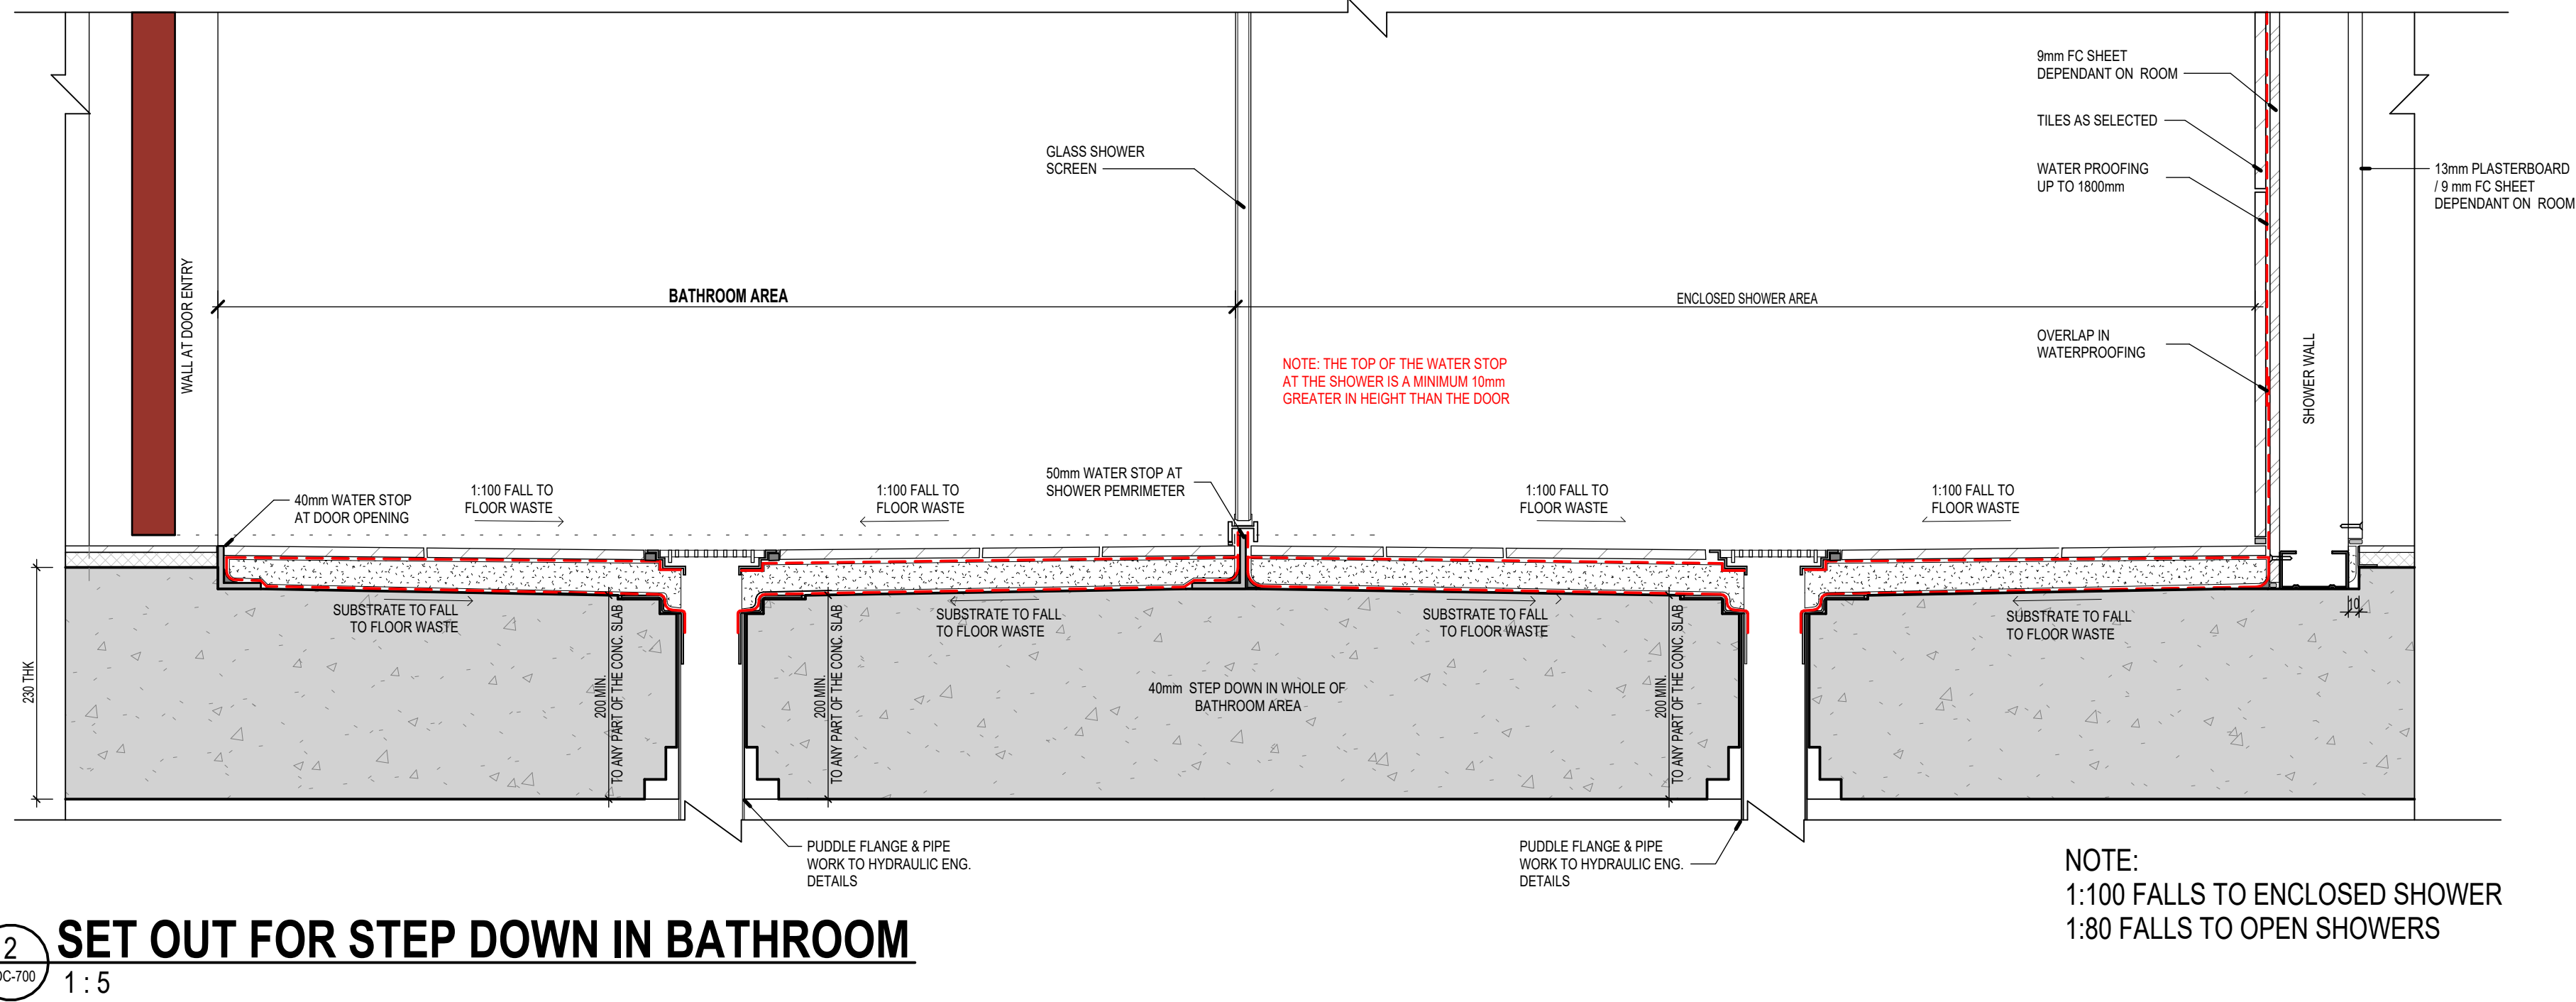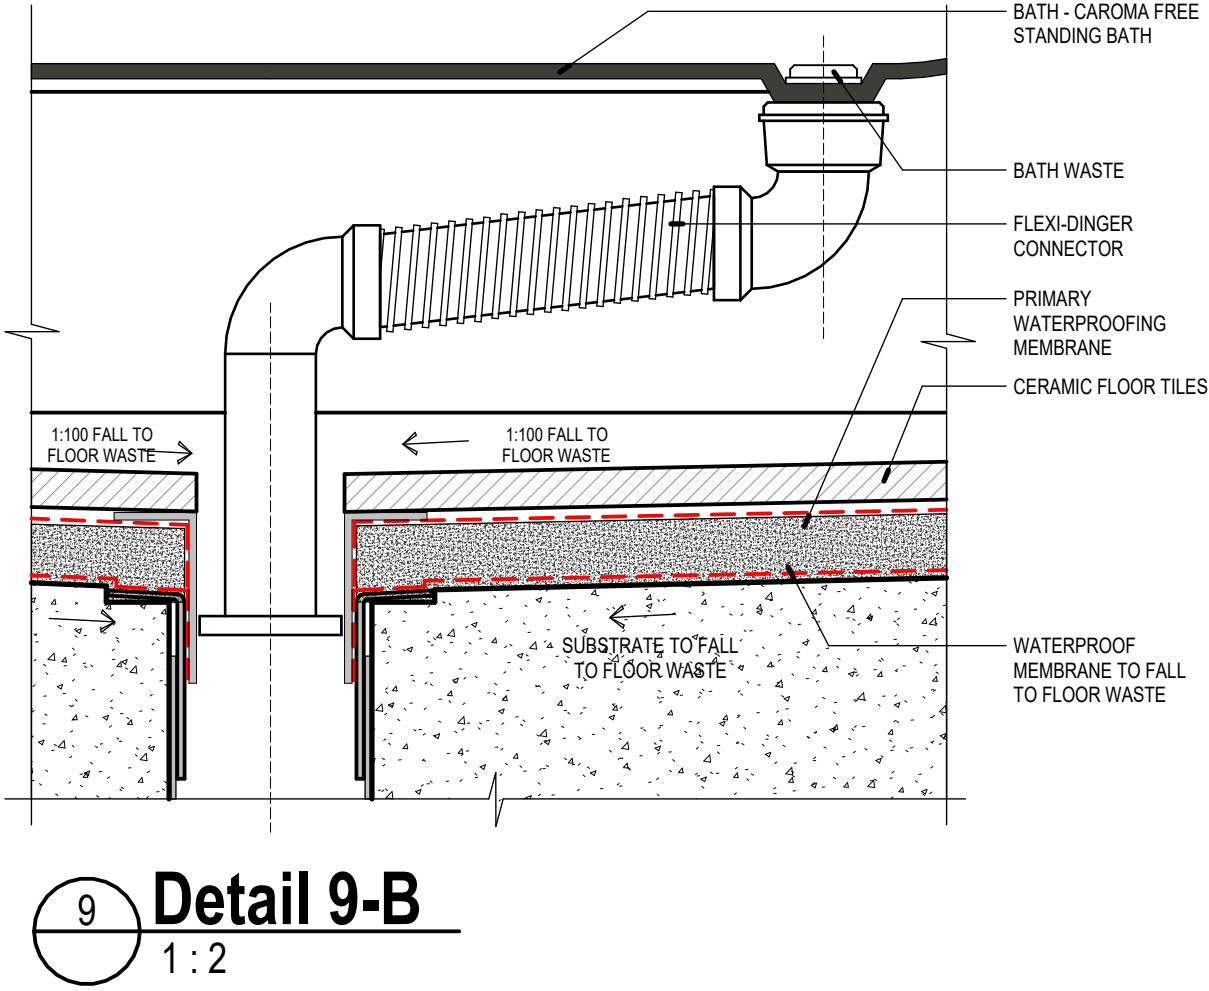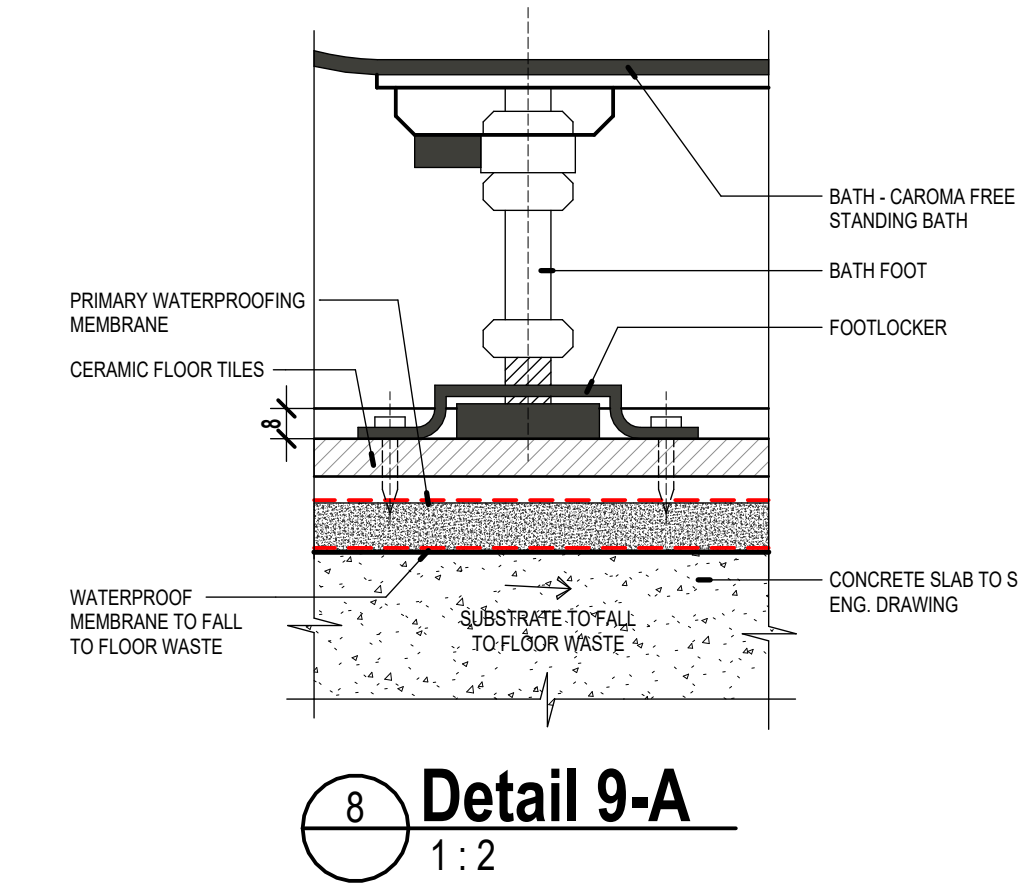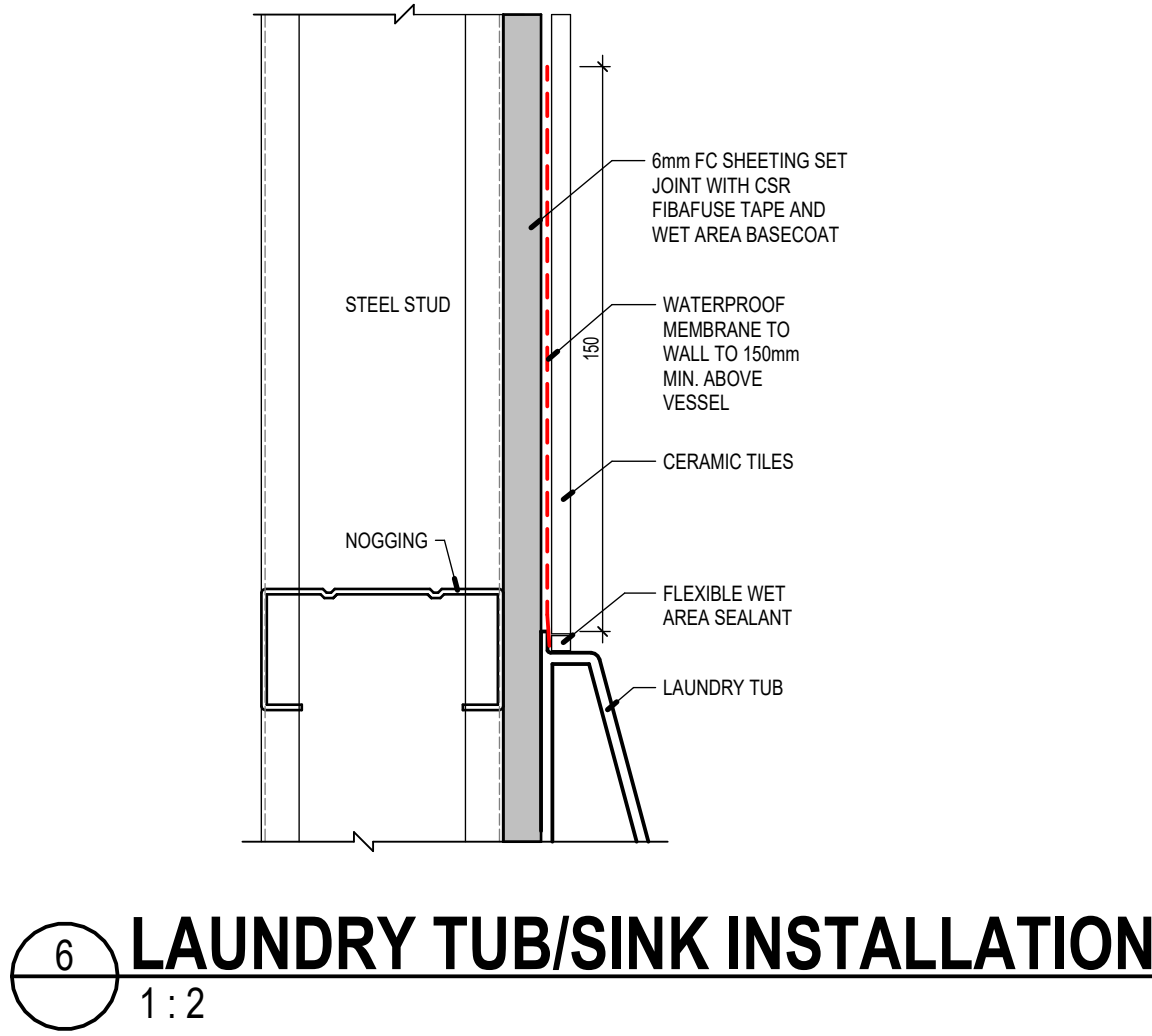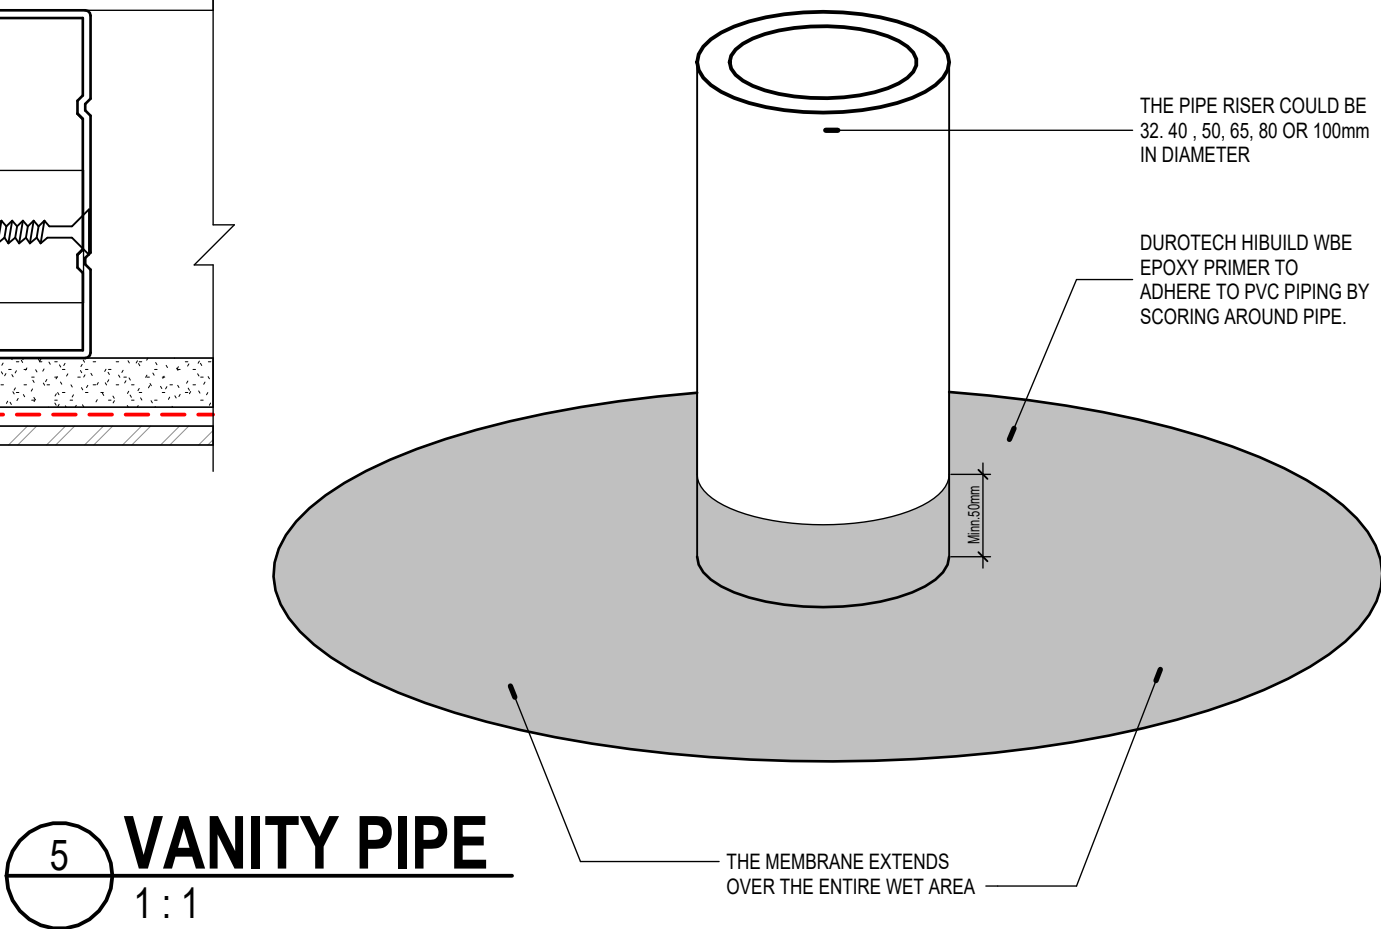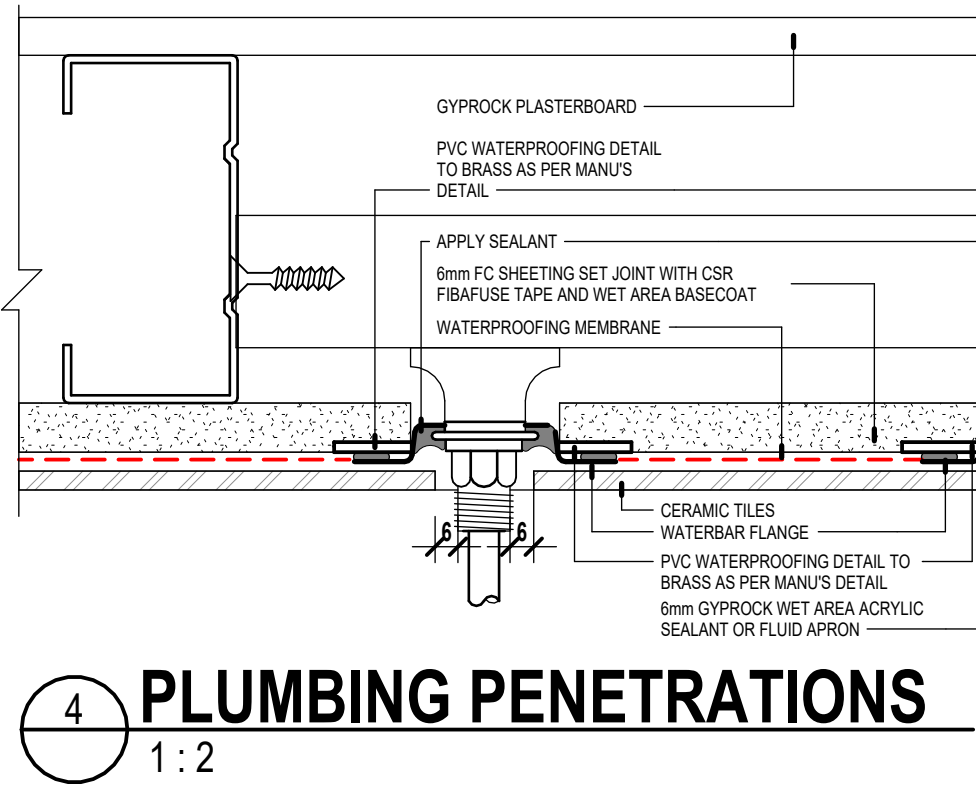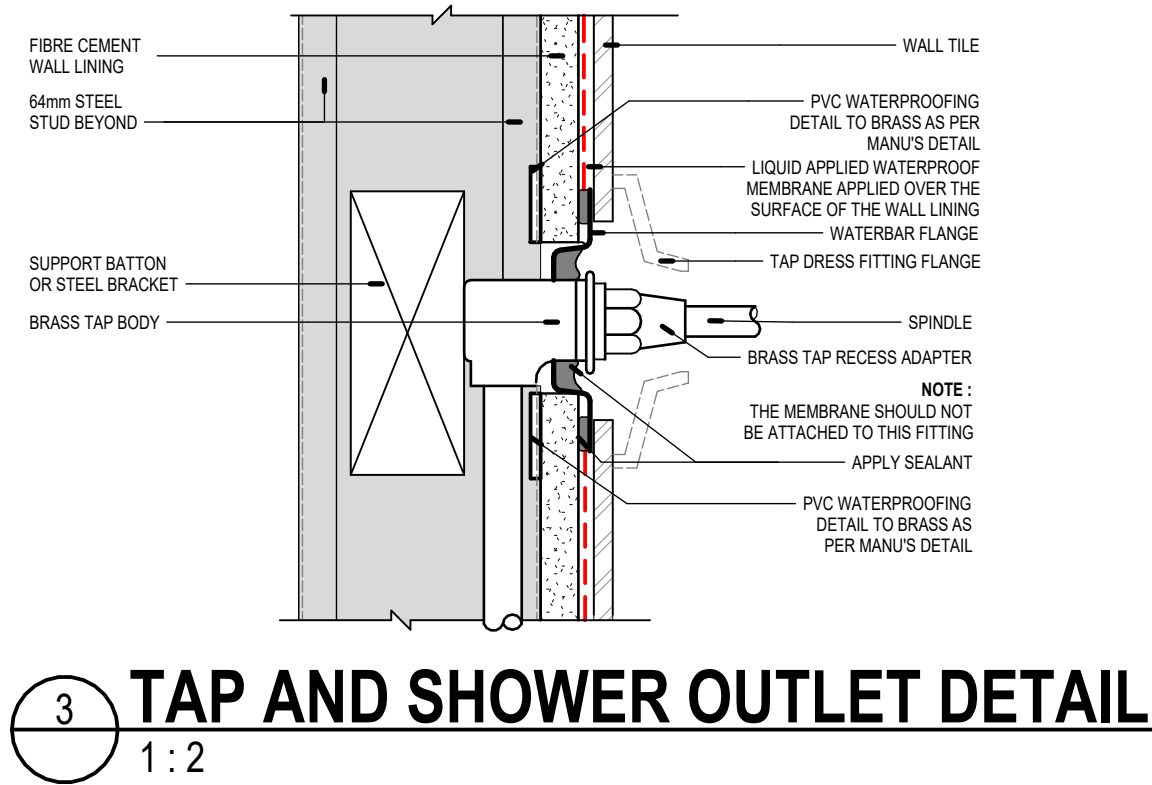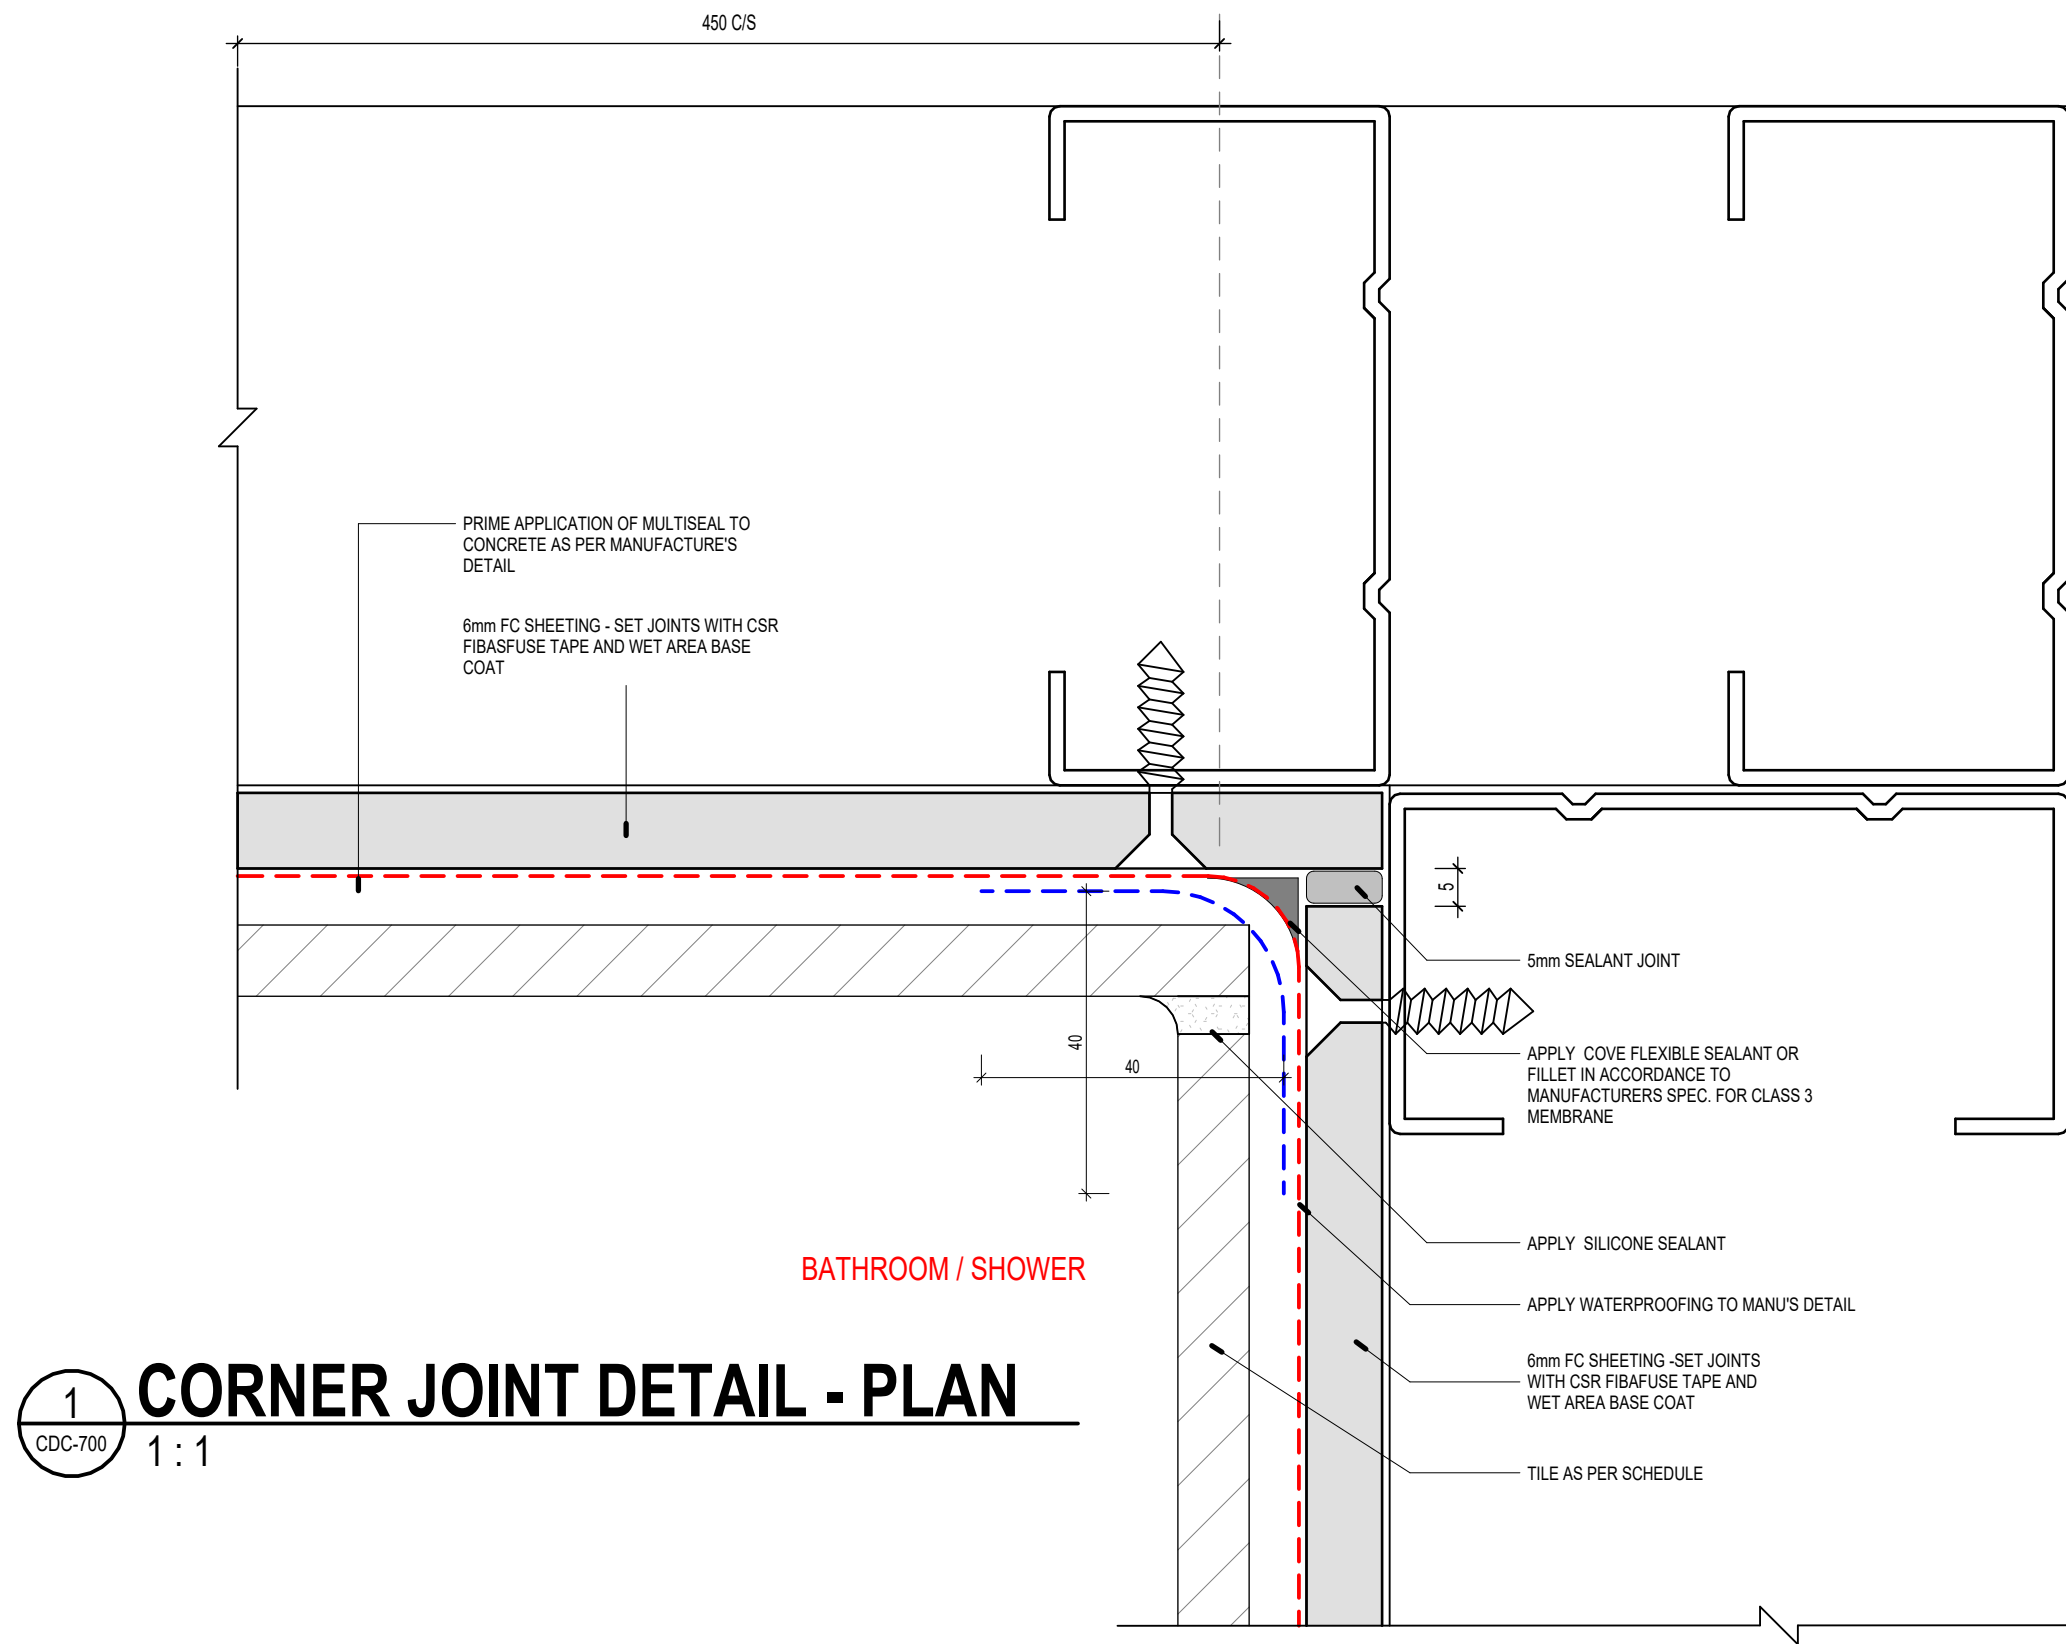

Beyond Certification (Sonder Projects Pty Ltd)
Reference: 3125176CDC
Date: 17/11/2025

Chen Wu
Certifier
BDC3224

COPYRIGHT & GENERAL NOTE:
Figured dimensions shall be taken in preference to scaling. Drawing to be read in conjunction with information on first page. Check all dimensions and levels on site before commencing work or ordering materials. All existing ground lines & levels location are approximate, therefore, to be verified on-site by the builder. Any discrepancies to be verified back to Zhin Architects before proceeding. All workmanship and materials shall comply with all relevant codes, ordinances, Australian Standards and manufacturers instructions. Unless noted issued for Construction drawing not to be used for construction. All art / graphic representations are indicative only. Information on this drawing is the copyright of Zhin Architects. Copying or using this drawing in whole or part without written permission infringes copyright.

C	ISSUE FOR CDC SUBMISSION 3	7/11/2025	TH	IC
B	ISSUE FOR CDC SUBMISSION 2	28/10/2025	TH	IC
A	ISSUE FOR CDC SUBMISSION	18/09/2025	TH	IC
ISSUE	AMENDMENT	DATE	DRAWN	CHECK

Drawing is NOT VALID or issued for use, unless checked

PROJECT ARCHITECTS
IAN CONRY

REGISTRATION NUMBER
NSW No. 8317



Zhin Architects Pty Ltd
Suite 1, Level 2
2 Rowe Street
Eastwood, NSW 2122
+61 2 8893 8888 / 0
info@zhin.com.au / 6
www.zhin.com.au / 4
28 495 869 790 / abn




PROJECT STATUS:
Complying Development Certificate

PROJECT NAME
Dual Occupancy

3 Johnston Ave
Kirrawee, NSW 2232
L.G.A.: SUTHERLAND SHIRE COUNCIL

SHEET TITLE
WET AREA DETAILS 2

Checked
Checker
8848
JOB No.
CDC-701
DRAWING No.
SCALE @A1 SHEET
As indicated
C
ISSUE
scale 1:100 @A1 sheet
10

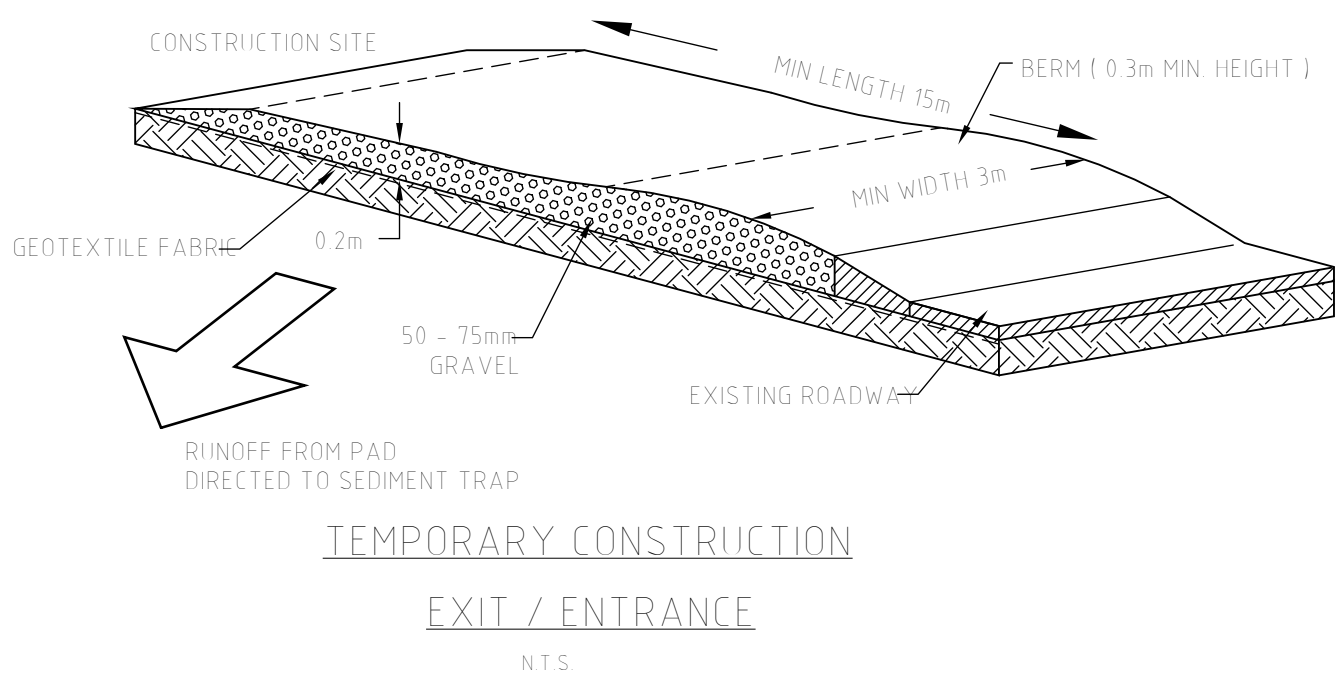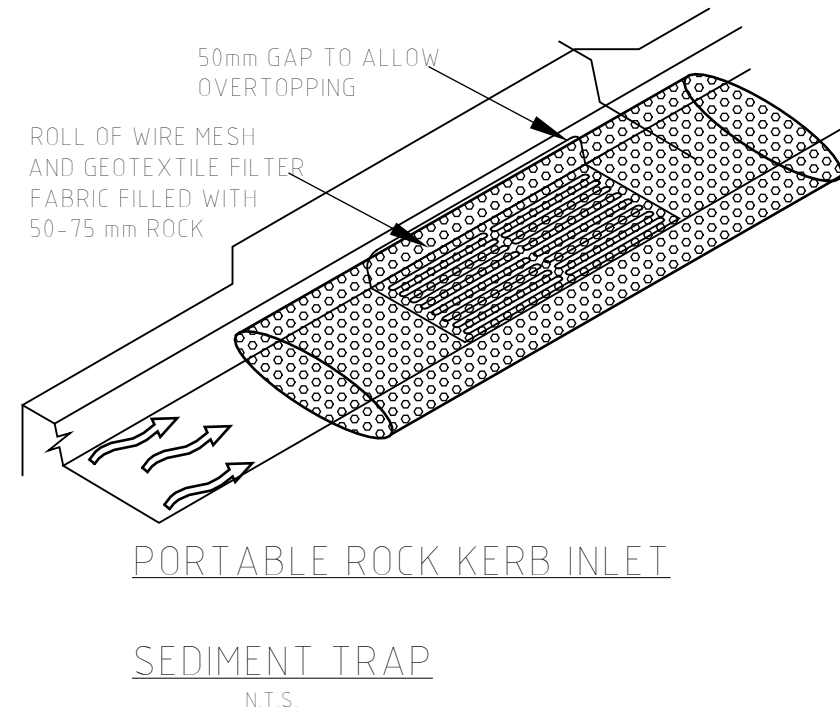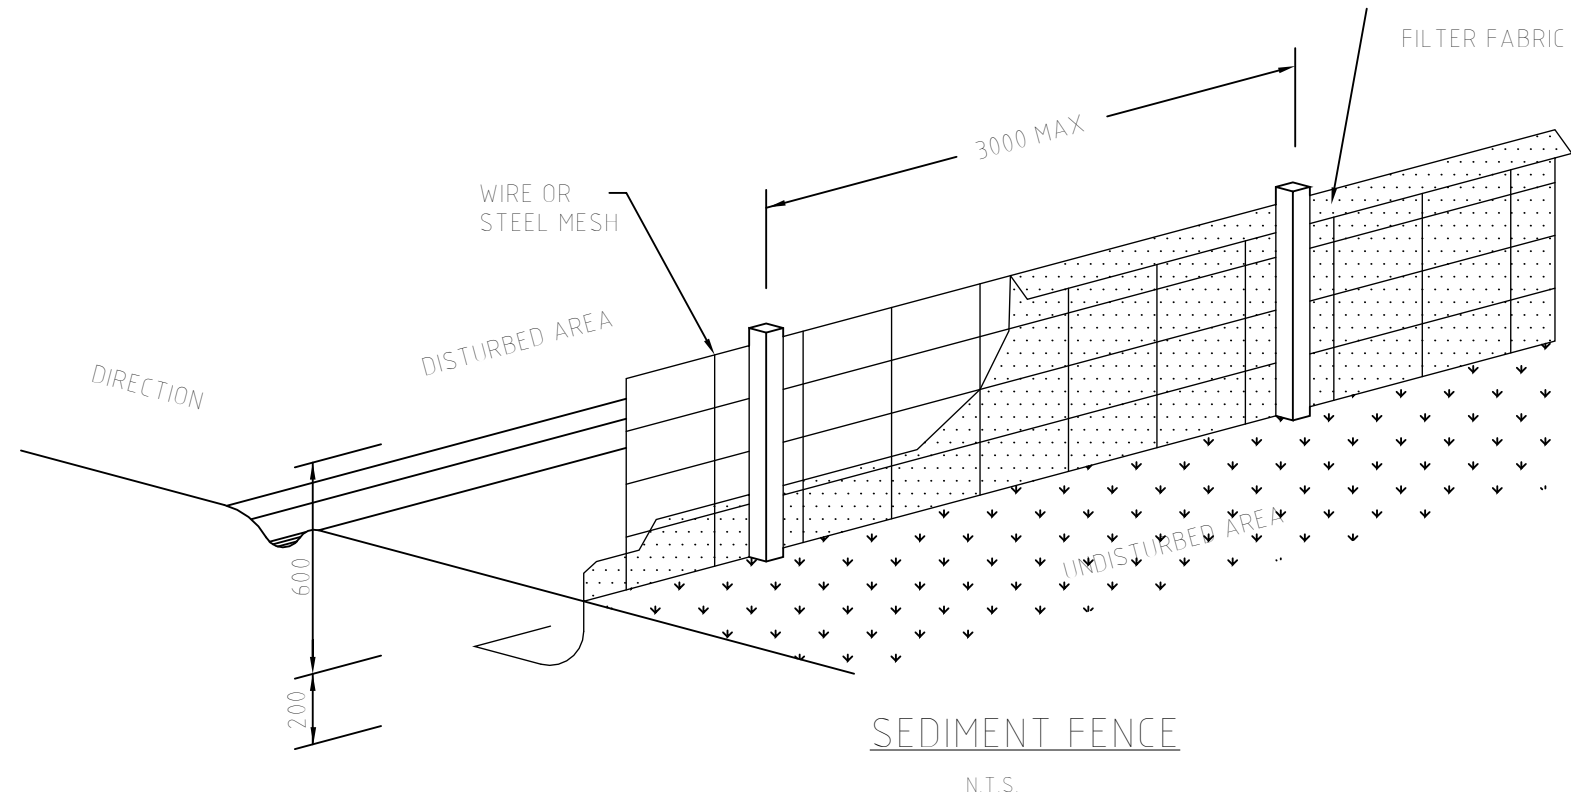

Typical Silt Protection Measures - NTS

See Stormwater Engineering Plans for additional detail

CONSTRUCTION MANAGEMENT PROGRAM

ALL STAGES

SITE / SECURITY FENCING AND SEDIMENT BARRICADES TO BE ERECTED PRIOR TO ANY OTHER WORKS. ALL PLANT AND EQUIPMENT TO BE KEPT AND OPERATED WHOLLY WITHIN THE SITE BOUNDARY.

SEE SITE PLAN FOR THE PLACEMENT OF SITE OFFICE, STAFF AMENITIES, TEMPORARY CAR PARKING, TRUCK UNLOADING AREAS, MATERIALS STORAGE AREAS, DUST AND MUD MINIMISATION MEASURES, INTERNAL VEHICLE CIRCULATION PATH, EMERGENCY EVACUATION POINT, SITE SECURITY, PLACEMENT OF TRAFFIC/PEDESTRIAN CONTROL DEVICES, AND WASTE BINS.

STAGE 1 - EXCAVATION
PRIMARILY THE EXCAVATION OF THE SITE AND ASSOCIATED GROUND WORKS. THE PLAN DETAILS THE INITIAL PLANNING ARRANGEMENTS AND SITE LAYOUT. SITE MANAGER TO DETERMINE THE OPTIMUM TEMPORARY LOCATIONS FOR PLANT, EQUIPMENT AND MATERIALS STORAGE.

CONSTRUCTION OF THE BASEMENT LEVEL. REFER TO STRUCTURAL ENGINEERING PLANS FOR DEAD-LOAD PLACEMENT DURING CONSTRUCTION.

STAGE 2 - BACKFILL OVER BASEMENT
COMPLETION OF BASEMENT LEVEL, SLAB, RAIN WATER TANK. ONCE COMPLETE, STAFF VEHICLES, PLANT + EQUIPMENT AND SMALL MATERIALS TO BE STORED WITHIN THE BASEMENT. SOIL BACK-FILL TO NEW GROUND LEVEL WITHIN THE FRONT SET-BACK.

STAGE 3 - CONSTRUCTION
MAIN CONSTRUCTION OF BUILDINGS ABOVE GROUND LEVEL. STAGGERED DELETION / RECONSTRUCTION OF THE DRIVEWAY CROSSINGS.

NOTE:

WORKS DESCRIBED HERE DO NOT INCLUDE ANY CIVIL ENGINEERING WORKS EITHER WITHIN THE SEWER EASEMENT OR IN THE PUBLIC ROADWAY. PLANNING AND COORDINATION OF CIVIL / STREET WORKS BY OTHERS.

TEMPORARY PEDESTRIAN MANAGEMENT PROGRAM

ALL STAGES

NOTIFICATION IS TO BE DELIVERED TO LOCAL RESIDENTS OF WORKS PROGRAM. ALL OUTSIDE-SITE WORKS ARE TO BE SECURED AFTER HOURS (AS MUCH AS PRACTICABLE) FOR THE DURATION OF WORKS.

PEDESTRIANS ADJACENT TO THE SITE WILL BE PROTECTED BY THE FOLLOWING MEANS:

THE SITE WILL BE FENCED WITH CYCLONE WIRE MESH WITH DUST-FABRIC BACKING ALONG THE STREET BOUNDARY AND SIDE/REAR BOUNDARIES TO PREVENT BOTH UNAUTHORISED ACCESS AND TO CONTAIN DUST RAISED BY CROSS-BREEZES.

SIDE AND REAR BOUNDARIES WILL BE FITTED WITH SILT / RIN-OFF BARRIERS AS PER THE STORMWATER ENGINEERING DETAILS AND SEDIMENT AND EROSION CONTROL PLANS.

VEHICLE ACCESS GATES TO SWING INWARDS AWAY FROM THE STREET, AND VEHICLES CROSSING TO BE SUPERVISED BY THE DESIGNATED TRAFFIC WARDEN. VEHICLES WILL BE REQUIRED TO GIVE WAY TO PEDESTRIAN TRAFFIC BEFORE CROSSING, PARTICULARLY DURING EGRESS. TRAFFIC WARDEN WILL ALSO REQUIRE SITE VEHICLES TO GIVE WAY TO STREET TRAFFIC (RESIDENT AND VISITOR).

ALL EGRESSING SITE VEHICLES TO BE CHECKED FOR DUST / MUD AND TO BE CLEANED TO RTA STANDARDS BEFORE DEPARTING. WATER SPRAY OR MUD IS TO BE CONTAINED ON SITE WHERE POSSIBLE. OVERSPRAY AND SPLASHING OFF-SITE TO BE AVOIDED.

DURING ANY TRAFFIC CONTROL EVENT WITH TRAFFIC WARDEN OR STOP/GO LOLLIPOP EQUIPMENT, MEASURES ARE TO BE PLACED AND OPERATING BEFORE SITE VEHICLE INGRESS OR EGRESS. NOTIFICATION OF DELIVERY E.T.A. TO BE GIVEN TO SITE MANAGER AND/OR TRAFFIC WARDEN FOR PREPARATION TIME.

CONSTRUCTION - STAGE 3

NOTIFICATION IS TO BE DELIVERED TO LOCAL RESIDENTS OF DELETION OF EXISTING DRIVEWAYS AND THEIR REPLACEMENT.

PRIOR TO DEMOLITION, BARRICADES ARE TO BE PUT IN PLACE DIVERTING PEDESTRIAN TRAFFIC TO OPPOSITE FOOTPATH. IF BARRICADES ARE TO BE IN PLACE FOR MORE THAN DAYLIGHT HOURS, THEY ARE TO INCLUDE FLASHING WARNING LIGHTS FOR THE DURATION OF WORKS.

DURING WORKS OUTSIDE SITE AREA, TRAFFIC WARDEN IS TO PROVIDE SUPERVISION TO PROTECT PEDESTRIAN AMENITY AND TO ENFORCE PEDESTRIAN RIGHT-OF-WAY.

TRAFFIC FLOW PROGRAM

ALL STAGES

ALL TRUCKS AND DELIVERY VEHICLES TO APPROACH FROM **JOHNSTON AVE** MAKING A LEFT-HAND TURN INTO THE SITE AND THEY EXIT TURN LEFT ONTO **BEAUFORT ST.**

ALL STAFF AND TRADE VEHICLES TO APPROACH SITE AND PARK WITHIN DESIGNATED / APPROVED TEMPORARY SURFACE SPACES OR WITHIN BUILDING ONCE BASEMENT CONSTRUCTION COMPLETE.

STREET PARKING FOR STAFF / TRADE VEHICLES IS TO BE DISCOURAGED. STAFF CAR-POOLING AND PUBLIC TRANSPORT USE IS TO BE ENCOURAGED.

SITE INGRESS AND EGRESS OF STAFF VEHICLES TO BE ORDERLY AND OUTSIDE 'NORMAL' MORNING AND EVENING PEAK TRAFFIC FLOW PERIODS TO AVOID CONGESTION WHEN PRACTICABLE.

STAGE 1 - EXCAVATION:

ARRIVAL:

LADEN AND DELIVERY VEHICLES WILL PROCEED TO ENTRY GATE UNLOADING TO TAKE PLACE WITHIN SITE AREA TO DESIGNATED STORAGE.

UNLADEN TRUCKS (TO COLLECT EXCAVATION MATERIAL) WILL APPROACH GATE AND REVERSE ONTO SITE AWAITING PICK-UP. LOADING TO TAKE PLACE WITHIN SITE, IN DESIGNATED LOADING AREA.

DEPARTURE:

DURING EXCAVATION AND CONSTRUCTION, ALL VEHICLES WILL BE CHECKED FOR DUST / MUD AND BE WASHED DOWN BEFORE EXITING THE SITE, WHEN APPROPRIATE. MANAGEMENT OF LARGE VEHICLES EXITING THE SITE WILL BE OVERSEEN / MANAGED BY THE GATE CONTROLLER OR DESIGNATED TRAFFIC WARDEN RESPONSIBLE FOR ANY TEMPORARY TRAFFIC CLOSURE.

EXCAVATION EQUIPMENT AND VEHICLES TO BE GARAGED ON SITE DURING THIS STAGE. UNLADEN EXCAVATION TRUCKS TO BE STAGGERED ARRIVAL - NO WAITING IN THE STREET. UNLADEN EXCAVATION TRUCKS TO BE OVERSEEN AND DIRECTED INTO PLACE BY DESIGNATED TRAFFIC WARDEN.

FOR TRUCK REVERSE TURNS INTO GATE, STOP/GO LOLLIPOP CONTROLS MAY BE REQUIRED [REFER TO TRAFFIC REPORT]. SCHEDULING OF ARRIVAL TO BE COORDINATED WITH SITE MANAGER.

EXCAVATION CONDITIONS


THE FINISHED FLOOR LEVEL OF PROPOSED SLABS WERE RL 77.9 M (UNIT 3A) AND RL 79.0 (UNIT 3B) AND THE SITE PREPARATION WOULD LIKELY INVOLVE MINOR CUTTING AND FILLING.

BASED ON THE SUBSURFACE MATERIAL ENCOUNTERED IN THE BOREHOLES, THE EXCAVATIONS FOR THE SLAB AREA WOULD LIKELY BE IN FILL AND CLAYS SANDS WHICH SHOULD BE UNDERTAKEN USING A MEDIUM SIZE EXCAVATOR WITH MINOR RIPPING IF BANDS OF WEATHERED ROCK ARE PRESENT.

WHERE REQUIRED, ANY FILL MATERIAL SHALL BE PLACED IN LOOSE LAYERS WITH A THICKNESS NOT GREATER THAN 250MM AT A MOISTURE CONTENT IN THE RANGE -1% TO +3% OF THE STANDARD OPTIMUM MOISTURE CONTENT. THE FILL LAYERS SHALL BE COMPACTED TO A MINIMUM DRY DENSITY RATIO OF 98% STANDARD COMPACTION. PRIOR TO PLACEMENT OF FILL MATERIAL, ANY SOFT AND SATURATED SOILS SHALL BE REMOVED.

Beyond Certification (Sonder Projects Pty Ltd)
Reference: 3125176CDC
Date: 17/11/2025

Chen Wu
Certifier
BDC3224

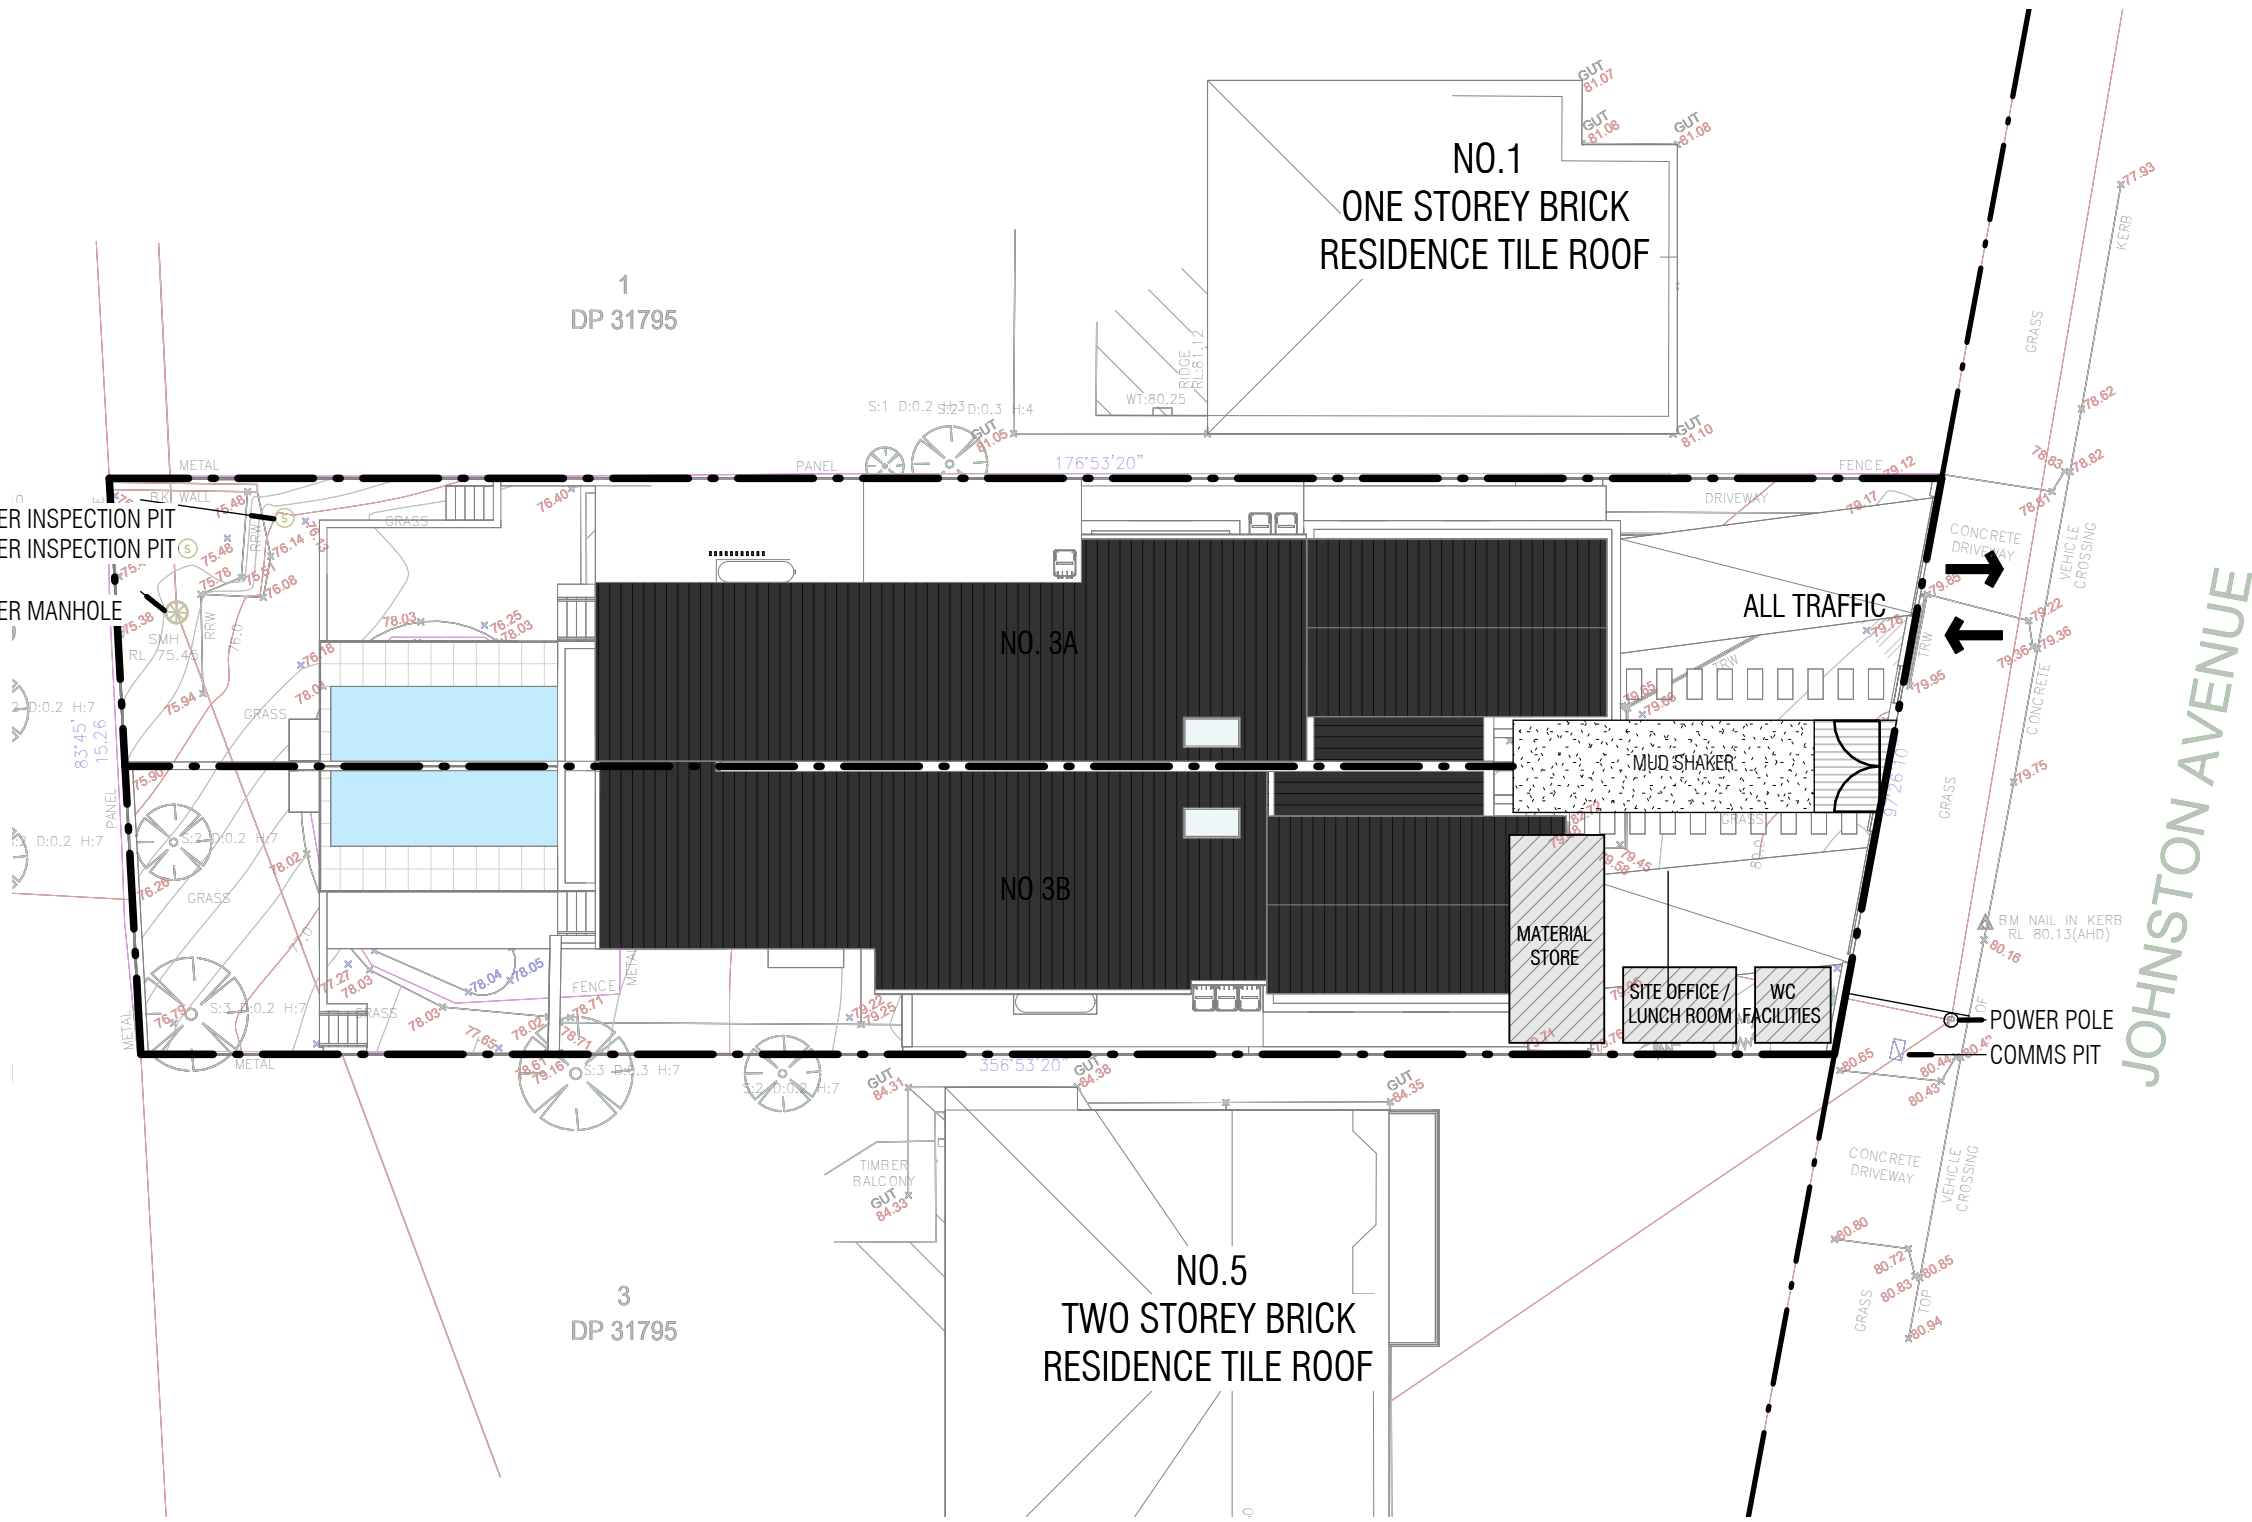

2 CONSTRUCTION MANAGEMENT PLAN CDC 103 1:200

COPYRIGHT & GENERAL NOTE:
Figured dimensions shall be taken in preference to scaling. Drawing to be read in conjunction with information on first page. Check all dimensions and levels on site before commencing work or ordering materials. All existing ground lines & levels location are approximate, therefore, to be verified on-site by the builder. Any discrepancies to be verified back to Zhin Architects before proceeding. All workmanship and materials shall comply with all relevant codes, ordinances, Australian Standards and manufacturers' instructions. Unless noted issued for Construction drawing not to be used for construction. All art / graphic representations are indicative only. Information on this drawing is the copyright of Zhin Architects. Copying or using this drawing in whole or part without written permission infringes copyright.

C	ISSUE FOR CDC SUBMISSION 3	7/11/2025	TH	IC
B	ISSUE FOR CDC SUBMISSION 2	28/10/2025	TH	IC
A	ISSUE FOR CDC SUBMISSION	18/09/2025	TH	IC
ISSUE	AMENDMENT	DATE	DRAWN	CHECK

Drawing is NOT VALID or issued for use, unless checked

PROJECT ARCHITECTS
IAN CONRY



REGISTRATION NUMBER
NSW No. 8317



Zhin Architects Pty Ltd

Suite 1, Level 2
2 Rowe Street
Eastwood, NSW 2122

+61 2 8893 8888 / o
info@zhin.com.au / o
www.zhin.com.au / o
28 495 869 790 / abn

PROJECT STATUS:

Complying Development Certificate

PROJECT NAME

Dual Occupancy

3 Johnston Ave

Kirrawee, NSW 2232

LGA: SUTHERLAND SHIRE COUNCIL

SHEET TITLE:

CONSTRUCTION MANAGEMENT PLAN

Checked
Checker

8848

JOB No.

CDC-702





DRAWING No.

SCALE @A1 SHEET
As indicated

C

ISSUE

scale 1:100 @A1sheet 10

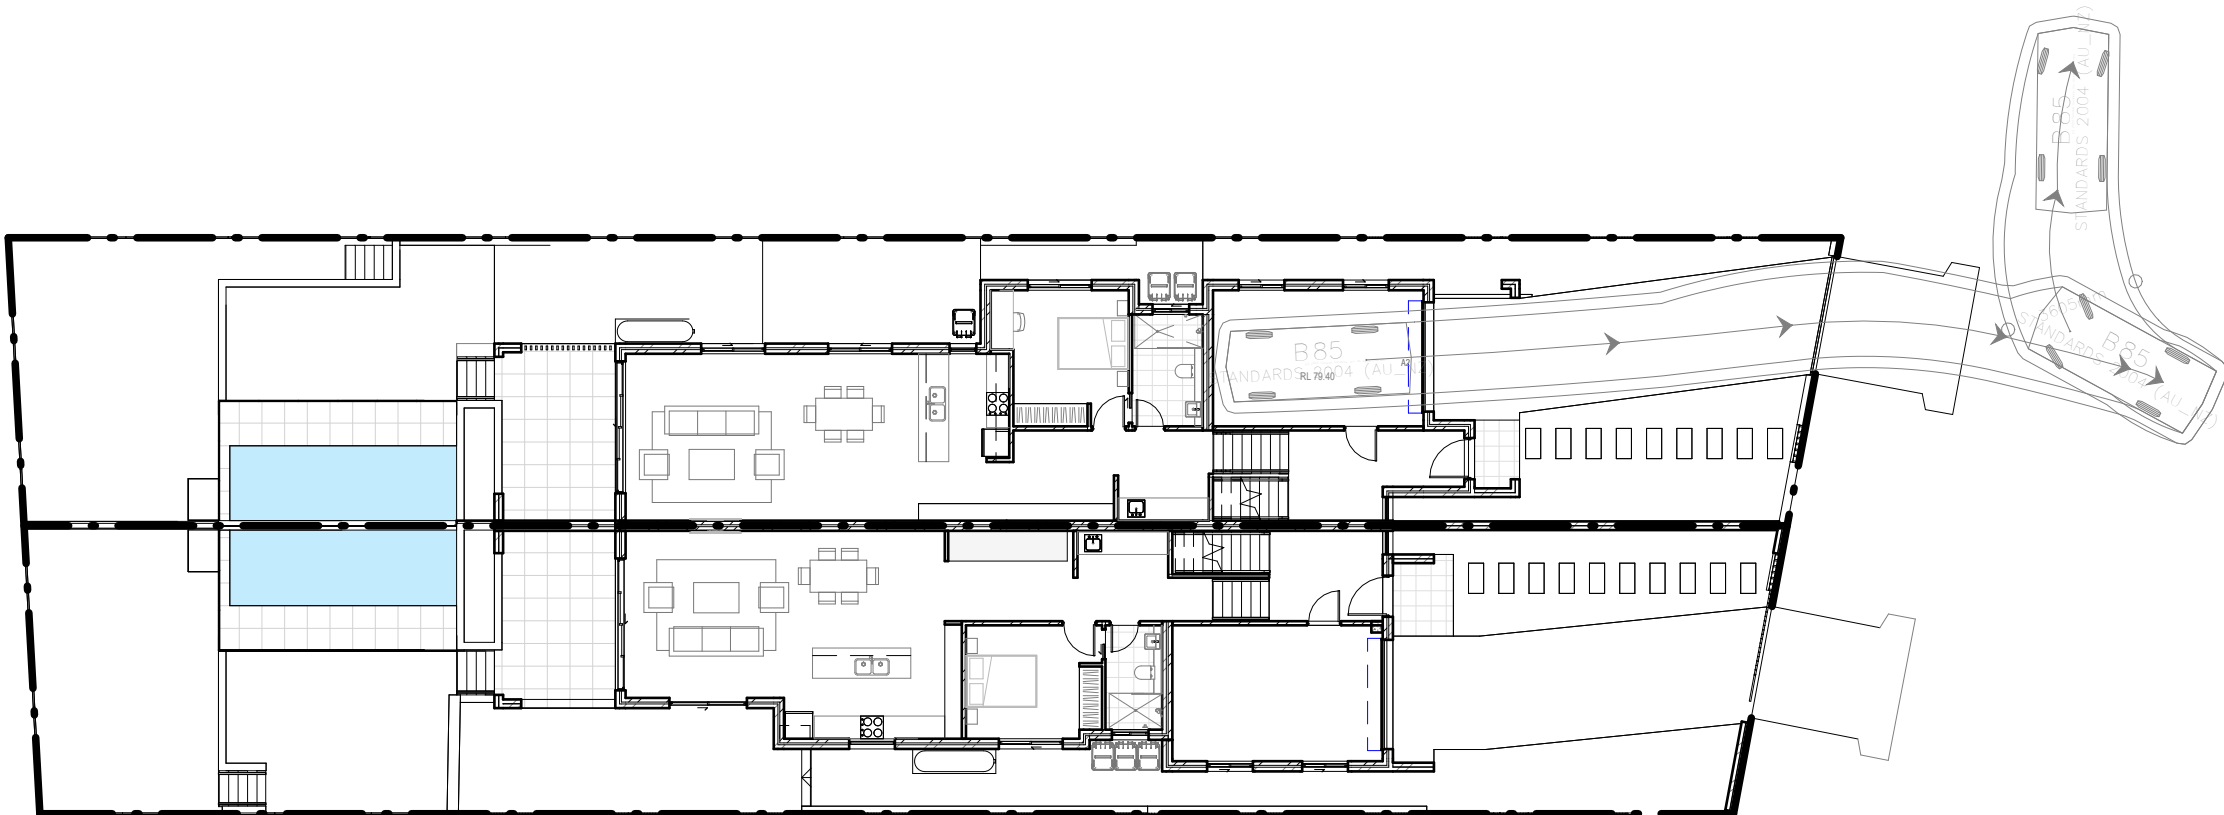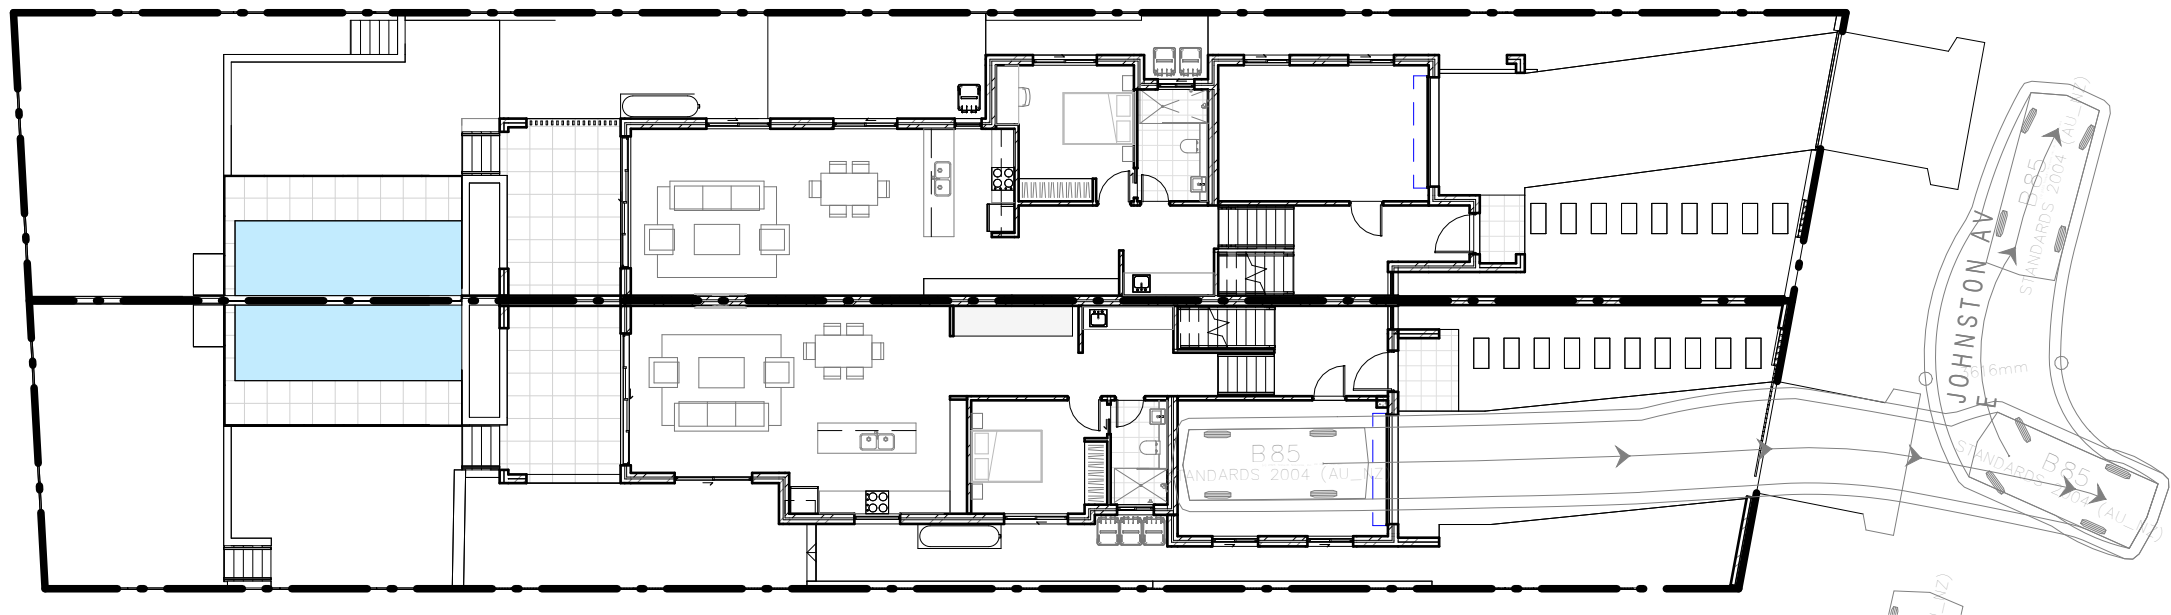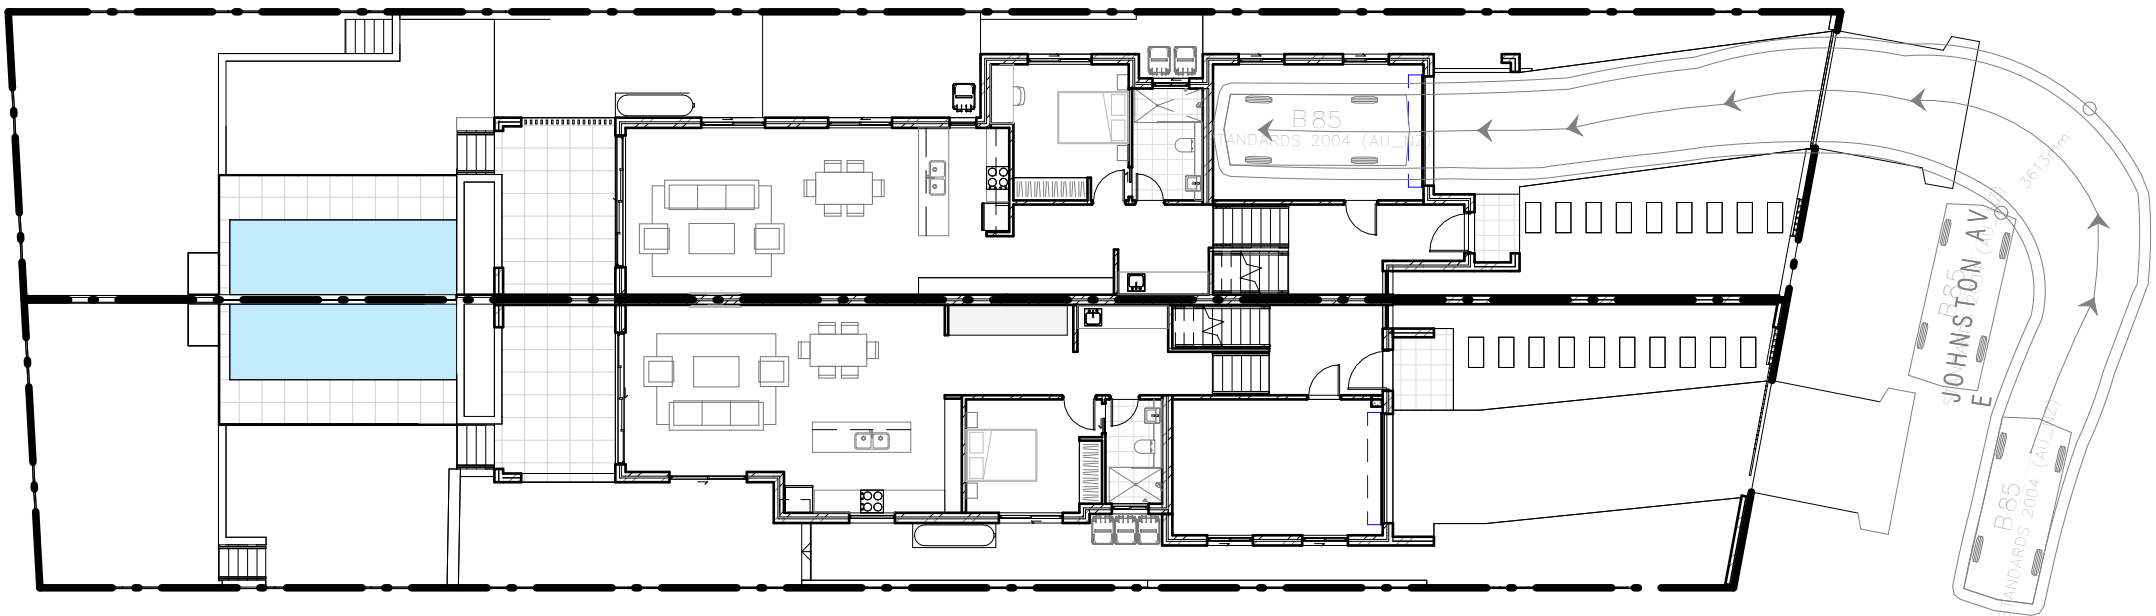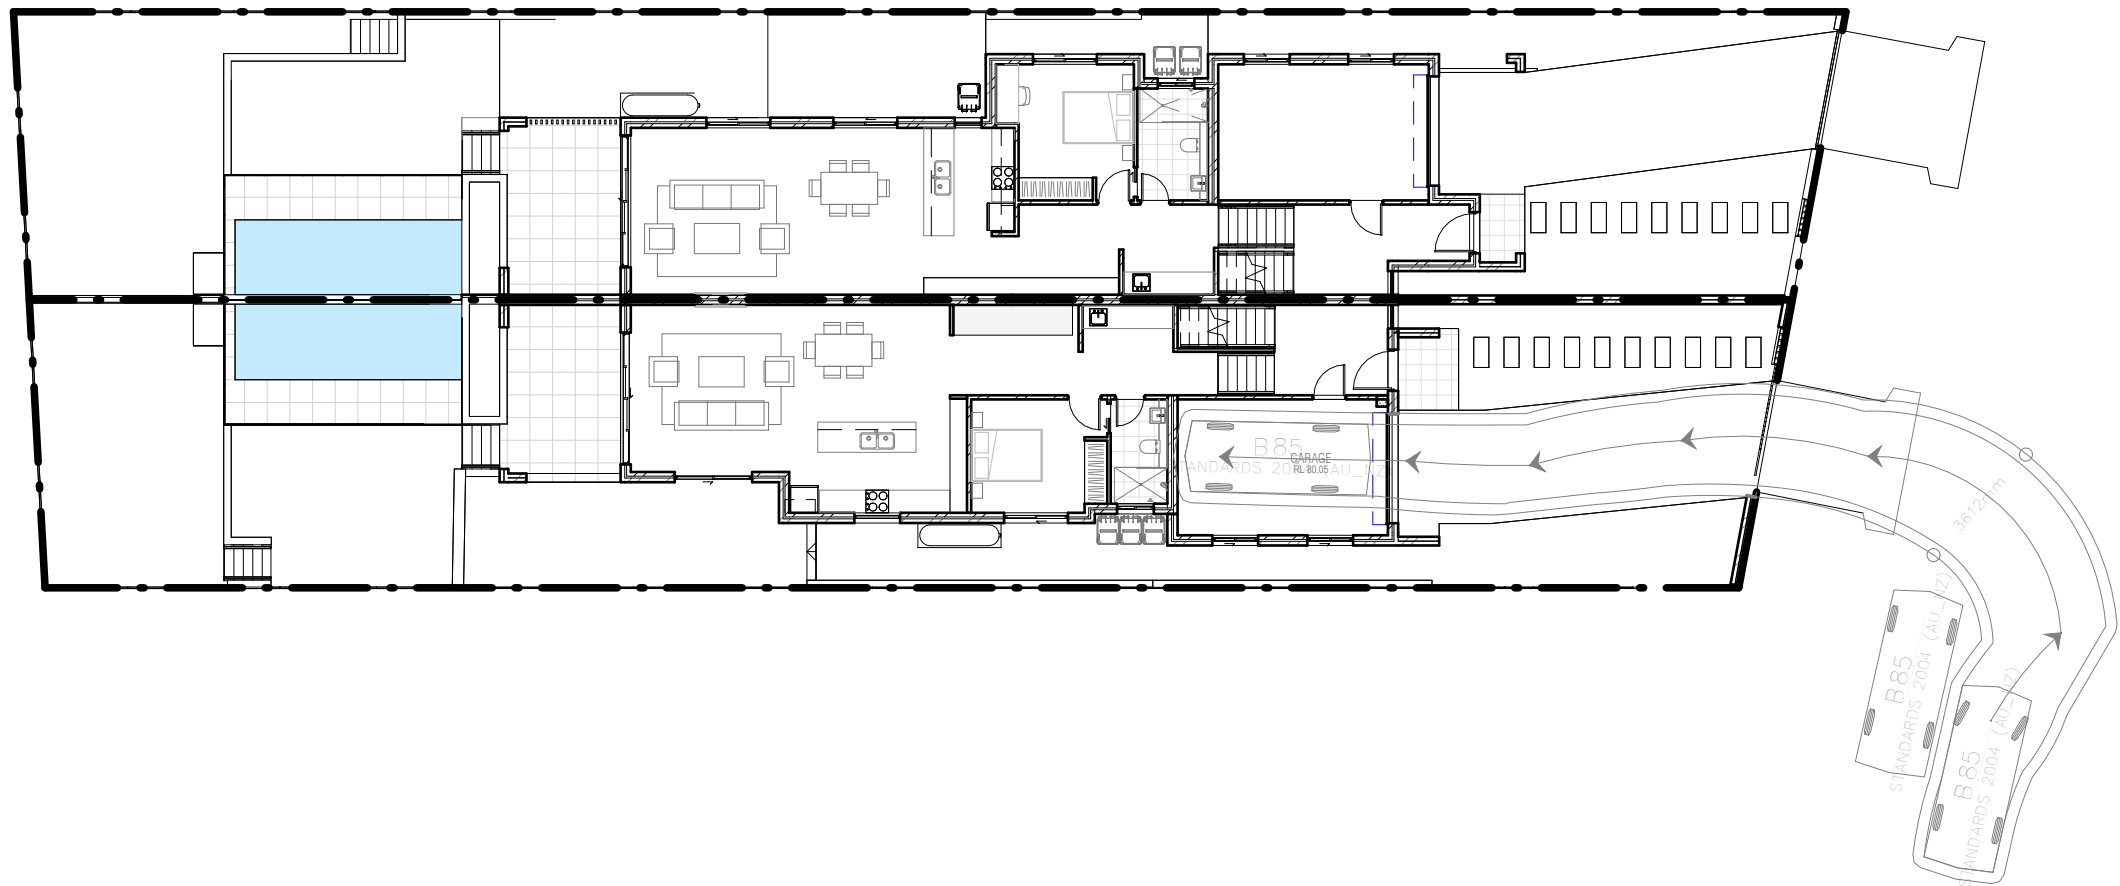

Beyond Certification (Sonder Projects Pty Ltd)
Reference: 3125176CDC
Date: 17/11/2025

Chen Wu
Certifier
BDC3224



COPYRIGHT & GENERAL NOTE:
Figured dimensions shall be taken in preference to scaling. Drawing to be read in conjunction with information on first page. Check all dimensions and levels on site before commencing work or ordering materials. All existing ground lines & levels location are approximate, therefore, to be verified on-site by the builder. Any discrepancies to be verified back to Zhinar Architects before proceeding. All workmanship and materials shall comply with all relevant codes, ordinances, Australian Standards and manufacturers' instructions. Unless noted issued for Construction drawing not to be used for construction. All art / graphic representations are indicative only. Information on this drawing is the copyright of Zhinar Architects. Copying or using this drawing in whole or part without written permission infringes copyright.

C	ISSUE FOR CDC SUBMISSION 3	7/11/2025	TH	IC
B	ISSUE FOR CDC SUBMISSION 2	28/10/2025	TH	IC
A	ISSUE FOR CDC SUBMISSION	18/09/2025	TH	IC
ISSUE	AMENDMENT	DATE	DRAWN	CHECK

Drawing is NOT VALID or issued for use, unless checked

PROJECT ARCHITECTS
IAN CONRY



REGISTRATION NUMBER
NSW No. 8317



Zhinar Architects Pty Ltd
Suite 1, Level 2
2 Rowe Street
Eastwood, NSW 2122
+61 2 8893 8888 / p
info@zhinar.com.au / e
www.zhinar.com.au / w
28 495 869 790 / abn

PROJECT STATUS:
Complying Development Certificate

PROJECT NAME
Dual Occupancy
3 Johnston Ave
Kirrawee, NSW 2232
L.G.A.: SUTHERLAND SHIRE COUNCIL

SHEET TITLE:
TRAFFIC SWEPHTH PATH

Checked
Checker

8848
JOB No.

CDC-800
DRAWING No.

SCALE @A1 SHEET
1 : 200
C
ISSUE

0 1 2 3 4 5 scale 1:100 @A1sheet 10