

FOR CONSTRUCTION

LOT 70 2 GOUNDREY STREET CATHERINE FIELDS

PROPOSED CONSTRUCTION OF A TWO STOREY DWELLING



BASIX COMMITMENTS		Certificate number: 1862748S_02 Date of issue: Tuesday, 15 September 2026
WATER		
LANDSCAPE	190m2	
TOILETS	4 STARS	
KITCHEN TAPS	4 STARS	
SHOWER HEADS	4 STAR (>4.5 but <=6 Umin)	
BASIN TAPS	4 STARS	
ALTERNATIVE WATER	1500L RAINWATER TANK	
ROOF WATER TO TANK	229m2	
ALT.WATER USES- TANK	LAUNDRY	
ALT. WATER USES - RETIC	ALL TOILETS + ONE OUTDOOR TAP	
SWIMMING POOL	N/A	
ENERGY		
HOT WATER	GAS INSTANTANEOUS - 6 STAR	
AIR-CON (HEATING)	3 PHASE DUCTED - EER 3.0-3.5	
AIR-CON (COOLING)	3 PHASE DUCTED - EER 3.0-3.5	
VENTILATION - BATHROOM	NONE/ NATURAL VENTILATION	
VENTILATION - KITCHEN	DUCTED - MANUAL SWITCH	
VENTILATION - LAUNDRY	NONE/ NATURAL VENTILATION	
PV SYSTEM	N/A	
COOKTOP	GAS	
OVEN	ELECTRIC	
CLOTHES DRYING	OUTDOOR CLOTHESLINE	
LIGHTING	DEDICATED LED	

GENERAL LEGEND	
AC	AIR CONDITIONING UNIT
AL	POWDERCOATED ALUMINIUM DOOR/ WINDOW
BAL	BALUSTRADE TYPE
BG	BOX GUTTER
BR1, BR2, etc.	BRICK FACE TYPE
CAP	METAL CAPPING
CD1, CD2, etc.	WALL CLADDING
CONC.	CONCRETE FLOOR
CPT	CARPET
CRT	CONCRETE ROOF TILES
CR1, CR2, etc.	CEMENT RENDER TYPE/ COLOUR
DP/S	DOWN PIPE
DW	DISH WASHER
ED	ENTRY DOOR
F	FRIDGE
FAS	FASCIA
FET	FEATURE TILE
FT, FT1, FT2, etc.	FLOOR TILES
FW	FLOOR WASTE
GD	GARAGE DOOR
GUT	GUTTER
HWU	HOT WATER UNIT
HYB	HYBRID FLOOR
L	LINEN
MR	METAL ROOF
MW	MICROWAVE OVEN
NGL	NATURAL GROUND LEVEL
OBS	OBSCURED GLASS
P	PANTRY
R	ROBE
RL	REDUCED LEVEL
RWH	RAIN WATER HEAD
RWT	RAIN WATER TANK
S	STORAGE
TOW	TOP OF WALL
TL	TIMBER LAMINATE
WC	WATER CLOSET
WM	WASHING MACHINE
SD	SMOKE DETECTOR

Sheet List				
Sheet No.	Sheet Name	Drawn By	Current Revision Date	Revision
CDC.01	COVER SHEET	AS	15-09-2026	CDC ISSUE
CDC.02A	GENERAL NOTES	AS	28-07-2026	CDC ISSUE
CDC.02B	GENERAL NOTES	AS	28-07-2026	CDC ISSUE
CDC.03	LOCATION PLAN AND SITE PLAN	AS	15-09-2026	CDC ISSUE
CDC.04	SITE ANALYSIS AND SEDIMENT CONTROL	AS	15-09-2026	CDC ISSUE
CDC.05	GROUND FLOOR PLAN	AS	15-09-2026	CDC ISSUE
CDC.06	FIRST FLOOR LEVEL	AS	15-09-2026	CDC ISSUE
CDC.07	ROOF PLAN	AS	15-09-2026	CDC ISSUE

Sheet List				
Sheet No.	Sheet Name	Drawn By	Current Revision Date	Revision
CDC.08	ELEVATION 01	AS	28-07-2026	CDC ISSUE
CDC.09	ELEVATION 02	AS	15-09-2026	CDC ISSUE
CDC.10	SECTIONS	AS	28-07-2026	CDC ISSUE
CDC.11	FLOOR AREA PLAN	AS	28-07-2026	CDC ISSUE
CDC.12	RENTABLE AREA PLAN	AS	28-07-2026	CDC ISSUE
CDC.14	COLOR SCHEDULE	AS	28-07-2026	CDC ISSUE
CDC.15	LANDSCAPE PLAN	AS	15-09-2026	CDC ISSUE
CDC.16	WATERPROOFING DETAILS	AS	28-07-2026	CDC ISSUE

NOTE.: ALL IMAGES ARE FOR ILLUSTRATION ONLY AND ARE SUBJECT TO VARIATION AS PER SITE CONDITION, STRUCTURAL ELEMENT AND TO AVAILABILITY OF MATERIALS.

9	15-09-2026	470x470 feature column added, FW6 shifted towards Secondary facade - Krishna	
8	7-09-2026	Feature columns removed - Ekta	
7	28-07-2026	CDC ISSUE	
6	16-07-2026	2 Awning Windows each to the Front on both floors, 2 double height rendered columns and horizontal connection on the Secondary Street side - Ekta.	
REV	DATE	DESCRIPTION	BY

THIS DRAWING IS THE EXCLUSIVE PROPERTY OF THE DEVELOPER & THE REPRODUCTION OF ANY PART WITHOUT THE PRIOR WRITTEN CONSENT OF THE DEVELOPER IS A VIOLATION OF APPLICABLE LAWS. IN NO EVENT SHALL THE DEVELOPER BE HELD LIABLE FOR SPECIAL COLLATERAL, INCIDENTAL OR CONSEQUENTIAL LIABILITY IN CONNECTION WITH THE USE OF THIS DIGITAL DATA ONCE RELEASED FROM THE DEVELOPER'S OFFICE. THIS DRAWING IS TO BE READ & UNDERSTOOD IN CONJUNCTION WITH THE STRUCTURAL, MECHANICAL, ELECTRICAL & / OR ANY OTHER CONSULTANT'S DOCUMENTATION AS MAY BE APPLICABLE TO THE PROJECT PRIOR TO THE START OF ANY WORKS AND FOR ITS DURATION.

PROJECT:

2 GOUNDREY STREET

LOT 70 2 GOUNDREY STREET
CATHERINE FIELDS

DRAWING TITLE:

COVER SHEET

NORTH:

LOT NO:	DATE:	SCALE:	DRAWING No:	REV:
70	15-09-2026	As indicated	CDC.01	9
DRAWN BY:	CHECKED BY:			ISSUED BY:
AS	RH			
DRAFTED BY:	CLIENT NAME:			
SL	Gopal Narayanappa & Shobha Srinivas Reddy			

CDC ISSUE

BUILDING SPECIFICATIONS

National Construction Code – Volume 2,
Amendment 1 – Building Code of Australia 2022
& Housing Provisions Standard 2022

SITE PREPARATION

- PART 3.1 OF THE NCC VOLUME 2, AMENDMENT 1 - BUILDING CODE OF AUSTRALIA 2022 & HOUSING PROVISIONS STANDARD 2022

EARTHWORKS

- TO BE CARRIED OUT IN ACCORDANCE WITH THE REQUIREMENTS OF THE ENVIRONMENTAL PLANNING & ASSESSMENT ACT 1979 AND DEVELOPMENT CONSENT CONDITIONS
- PART 3.2 OF THE NCC VOLUME 2, AMENDMENT 1 - BUILDING CODE OF AUSTRALIA 2022 & HOUSING PROVISIONS STANDARD 2022.
- AS 4678:2002 - EARTH-RETAINING STRUCTURES

DRAINAGE

- PART 3.3 OF THE NCC VOLUME 2, AMENDMENT 1 - BUILDING CODE OF AUSTRALIA 2022 & HOUSING PROVISIONS STANDARD 2022.
- AS/NZS 3500.1:2021 - PLUMBING & DRAINAGE - WATER SERVICES
- AS/NZS 3500.2:2021 - PLUMBING & DRAINAGE - SANITARY PLUMBING & DRAINAGE
- AS/NZS 3500.3:2021 - PLUMBING & DRAINAGE STORMWATER DRAINAGE
- AS/NZS 3500.4:2021 - PLUMBING & DRAINAGE - HEATED WATER SERVICES

STRUCTURAL WORK

- Part 2.2 OF THE NCC VOLUME 2, AMENDMENT 1 - BUILDING CODE OF AUSTRALIA 2022 & HOUSING PROVISIONS STANDARD 2022.
- AS 4100:2020 - STEEL STRUCTURES CODES
- AS/NZS 1170.0:2002 - GENERAL PRINCIPLES
- AS/NZS 1170.1:2002 - PARTS 1 PERMANENT, IMPOSED AND OTHER ACTIONS
- AS/NZS 1170.2:2021 - PART 2 WIND ACTIONS
- AS 3700:2018 - SAA MASONRY CODE
- AS 1684.3:2021 - RESIDENTIAL TIMBER FRAMED CONSTRUCTION

FOOTINGS & SLABS

- PART 4 OF THE NCC VOLUME 2, AMENDMENT 1 - BUILDING CODE OF AUSTRALIA 2022 & HOUSING PROVISIONS STANDARD 2022.
- AS 2159:2009 - PILING - DESIGN & INSTALLATION
- AS 2870:2011 - RESIDENTIAL SLABS & FOOTINGS
- AS 3600:2018 - CONCRETE STRUCTURES

MASONRY

- PART 5 OF THE NCC VOLUME 2, AMENDMENT 1 - BUILDING CODE OF AUSTRALIA 2022 & HOUSING PROVISIONS STANDARD 2022.
- AS 3700:2018 - MASONRY STRUCTURES
- PART 6 OF THE NCC VOLUME 2, AMENDMENT 1 - BUILDING CODE OF AUSTRALIA 2022 & HOUSING PROVISIONS STANDARD 2022.
- AS 1684.2:2021 - RESIDENTIAL TIMBER-FRAMED CONSTRUCTION - NON- CYCLONIC AREAS
- AS 1720.1:2010 - TIMBER STRUCTURES - DESIGN METHODS
- AS 4100:2020 - STEEL STRUCTURES
- AS 3660.1:2014 - TERMITE MANAGEMENT SYSTEM

ROOF & WALL CLADDING

- PART 7 OF THE NCC VOLUME 2, AMENDMENT 1 - BUILDING CODE OF AUSTRALIA 2022 & HOUSING PROVISIONS STANDARD 2022.
- AS 1273:1991 - UNPLASTICIZED PVC (UPVC) DOWNPIPES & FITTINGS FOR RAINWATER
- AS 1562.1:2018 - DESIGN & INSTALLATION OF SHEET ROOF & WALL CLADDING - METAL
- AS/NZS 1562.3:2006 - DESIGN & INSTALLATION OF SHEET ROOF & WALL CLADDING - PLASTIC
- AS 2049:2002 - ROOF TILES
- AS 2050:2018 - INSTALLATION OF ROOF TILES
- AS 4285:2019 - ROOFLIGHTS

GLAZING

- PART 8 OF THE NCC VOLUME 2, AMENDMENT 1 - BUILDING CODE OF AUSTRALIA 2022 & HOUSING PROVISIONS STANDARD 2022.
- AS 1288:2021 - GLASS IN BUILDINGS - SELECTION & INSTALLATION
- AS 2047:2014 - WINDOWS & EXTERNAL GLAZED DOORS IN BUILDINGS
- AS/NZS 2208:1996 - SAFETY GLAZING MATERIALS IN BUILDINGS

FIRE SAFETY

- PART 9 OF THE NCC VOLUME 2, AMENDMENT 1 - BUILDING CODE OF AUSTRALIA 2022 & HOUSING PROVISIONS STANDARD 2022.
- AS 3786:2014 - SMOKE ALARMS USING SCATTERED LIGHT, TRANSMITTED LIGHT OR IONIZATION

HEALTH & AMENITY

- PART 10 OF THE NCC VOLUME 2, AMENDMENT 1 - BUILDING CODE OF AUSTRALIA 2022 & HOUSING PROVISIONS STANDARD 2022.
- AS/NZS ISO 717.1:2004 - ACOUSTICS - RATING OF SOUND INSULATION IN BUILDINGS & OF BUILDING ELEMENTS - AIRBORNE SOUND INSULATION
- AS ISO 717.2:2004 - ACOUSTICS - RATING OF SOUND INSULATION IN BUILDINGS & OF BUILDING ELEMENTS - IMPACT SOUND INSULATION
- AS 1668.2:2012 - THE USE OF VENTILATION & AIR CONDITIONING IN BUILDINGS - MECHANICAL VENTILATION IN BUILDINGS
- AS 1668.4:2012 - THE USE OF VENTILATION & AIR CONDITIONING IN BUILDINGS - NATURAL VENTILATION OF BUILDINGS
- AS/NZS 1680.0:2009 - INTERIOR LIGHTING - SAFE MOVEMENT
- AS 3740:2021 - WATERPROOFING OF DOMESTIC WET AREAS
- AS 3000:2018 - ELECTRICAL INSTALLATION
- BCA Part 10.8.1, AS4200.1 & AS4200.2 - PLIABLE BUILDING MEMBRANE INSTALLED.

WATERPROOFING

- PART 10.2 OF THE NCC VOLUME 2, AMENDMENT 1 - BUILDING CODE OF AUSTRALIA 2022 & HOUSING PROVISIONS STANDARD 2022
- AS 3740:2021 - WATERPROOFING TO WET AREA
- AS 4654:2012 - EXTERNAL WET AREAS

SAFE MOVEMENT & ACCESS

- PART 11 OF THE NCC VOLUME 2, AMENDMENT 1 - BUILDING CODE OF AUSTRALIA 2022 & HOUSING PROVISIONS STANDARD 2022.
- AS 1428.1:2009 - DESIGN FOR ACCESS & MOBILITY - GENERAL REQUIREMENTS FOR ACCESS - NEW BUILDING WORK
- AS 1657:2018 - FIXED PLATFORMS, WALKWAYS, STAIRWAYS & LADDERS - DESIGN, CONSTRUCTION & INSTALLATION

HANDRAILS & BALUSTRADE

- PART 11.3.3 OF THE NCC VOLUME 2, AMENDMENT 1 - BUILDING CODE OF AUSTRALIA 2022 & HOUSING PROVISIONS STANDARD 2022.
- PART 11.3.4 OF THE NCC VOLUME 2, AMENDMENT 1 - BUILDING CODE OF AUSTRALIA 2022 & HOUSING PROVISIONS STANDARD 2022.
- PART 11.3.5 OF THE NCC VOLUME 2, AMENDMENT 1 - BUILDING CODE OF AUSTRALIA 2022 & HOUSING PROVISIONS STANDARD 2022.
- AS 1170.1:2002 - BALUSTRADE INSTALLATION

PROTECTION OF OPENABLE WINDOW


PART 11.3.7 AND 11.3.8 OF THE NCC VOLUME 2, AMENDMENT 1 - BUILDING CODE OF AUSTRALIA 2022 & HOUSING PROVISIONS STANDARD 2022.

ENERGY EFFICIENCY

- PART 13 OF THE NCC VOLUME 2, AMENDMENT 1 - BUILDING CODE OF AUSTRALIA 2022 & HOUSING PROVISIONS STANDARD 2022 & BASIX CERTIFICATE.

MECHANICAL VENTILATION

- EXHAUST FROM A BATHROOM, SANITARY COMPARTMENT TO DISCHARGE DIRECTLY TO OUTDOOR AIR WITH MINIMUM FLOW RATE OF 25L/S & MAKE-UP AIR VIA OPENINGS TO AN ADJACENT ROOM WITH A FREE AREA OF 14,000 MM². THIS EXHAUST SYSTEM MUST BE INTERLOCKED WITH LIGHT SWITCH AND INCLUDE RUN-ON TIMER SO THAT THE EXHAUST SYSTEM CONTINUES TO OPERATE FOR 10 MINUTES AFTER THE LIGHT SWITCH IS OFF.
- ANY INSTALLED - KITCHEN RANGEHOOD EXHAUST TO DISCHARGE DIRECTLY OR VIA DUCT TO OUTDOOR AIR WITH MINIMUM FLOW RATE OF 40L/S & MAKE-UP AIR VIA OPENINGS TO AN ADJACENT ROOM WITH A FREE AREA OF 14,000 MM².
- LAUNDRY EXHAUST TO DISCHARGE DIRECTLY OR VIA DUCT TO OUTDOOR AIR WITH MINIMUM FLOW RATE OF 40L/S & MAKE-UP AIR VIA OPENINGS TO AN ADJACENT ROOM WITH A FREE AREA OF 14,000 MM².

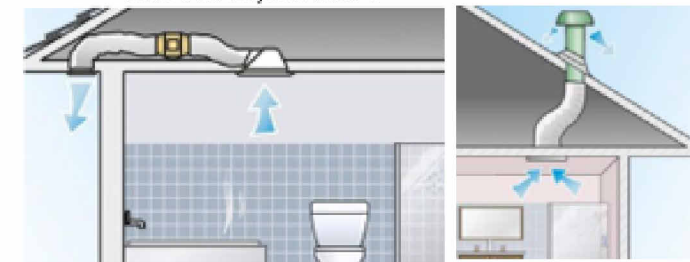

REV	DATE	DESCRIPTION	BY
7	28-07-2026	CDC ISSUE	



THIS DRAWING IS THE EXCLUSIVE PROPERTY OF THE DEVELOPER & THE REPRODUCTION OF ANY PART WITHOUT THE PRIOR WRITTEN CONSENT OF THE DEVELOPER IS A VIOLATION OF APPLICABLE LAWS. IN NO EVENT SHALL THE DEVELOPER BE HELD LIABLE FOR SPECIAL COLLATERAL, INCIDENTAL OR CONSEQUENTIAL LIABILITY IN CONNECTION WITH THE USE OF THIS DIGITAL DATA ONCE RELEASED FROM THE DEVELOPER'S OFFICE. THIS DRAWING IS TO BE READ & UNDERSTOOD IN CONJUNCTION WITH THE STRUCTURAL, MECHANICAL, ELECTRICAL & / OR ANY OTHER CONSULTANT'S DOCUMENTATION AS MAY BE APPLICABLE TO THE PROJECT PRIOR TO THE START OF ANY WORKS AND FOR ITS DURATION.

PROJECT:
2 GOUNDREY STREET

LOT 70 2 GOUNDREY STREET
CATHERINE FIELDS

DRAWING TITLE:
GENERAL NOTES


<u>NORTH:</u>	LOT NO:	DATE:	SCALE:	<u>DRAWING No:</u>	<u>REV:</u>
	70	15-09-2026	1 : 2	CDC.02A	7
	DRAWN BY:	CHECKED BY:			ISSUED BY:
	AS	RH			
DRAFTED BY:	CLIENT NAME:				
SL	Gopal Narayanappa & Shobha Srinivas Reddy				

CDC ISSUE

7


ISSUED BY:

- TERMITE SHEET EXTENDS THROUGH THE ENTIRE MASONRY LEAF AND IS VISIBLE AT THE FINISHED FACE OF THE WALL.

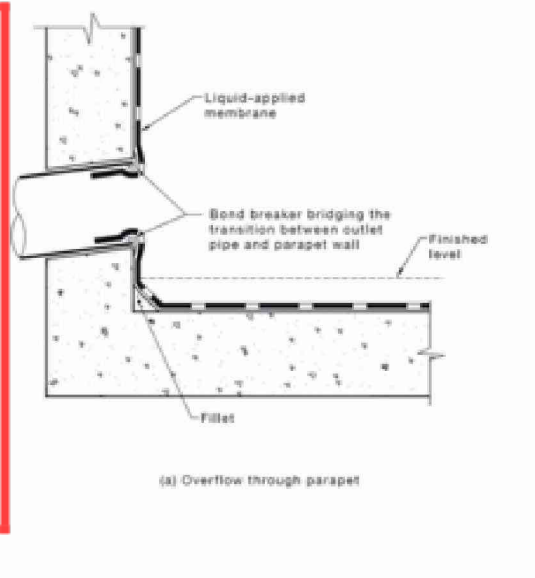

DPC FOR BRICKS

DAMP-PROOF COURSE (DPC) TO EXTENDS THROUGH THE ENTIRE MASONRY LEAF AND NEED TO BE VISIBLE AT THE FINISHED FACE OF THE WALL FROM OUTSIDE

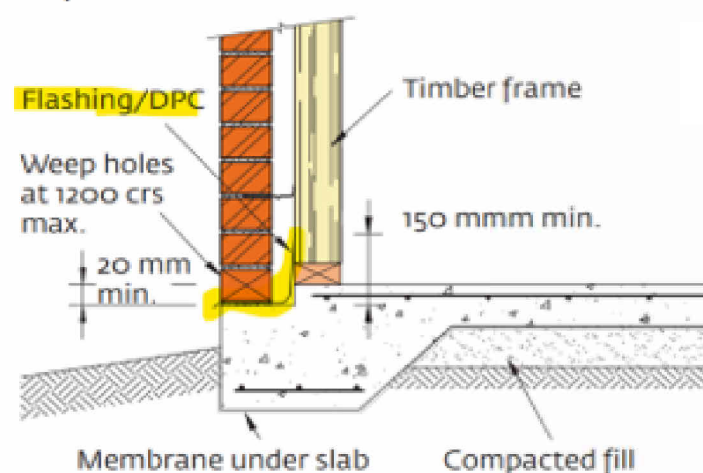

OVERFLOW TO BALCONY:

- SURFACE DRAIN & OVERFLOW TO BALCONY



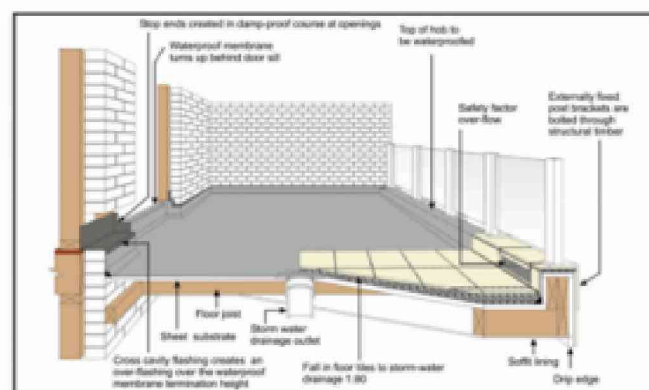


Figure 10.2.24: Typical bathroom door details for whole bathroom waterproofing

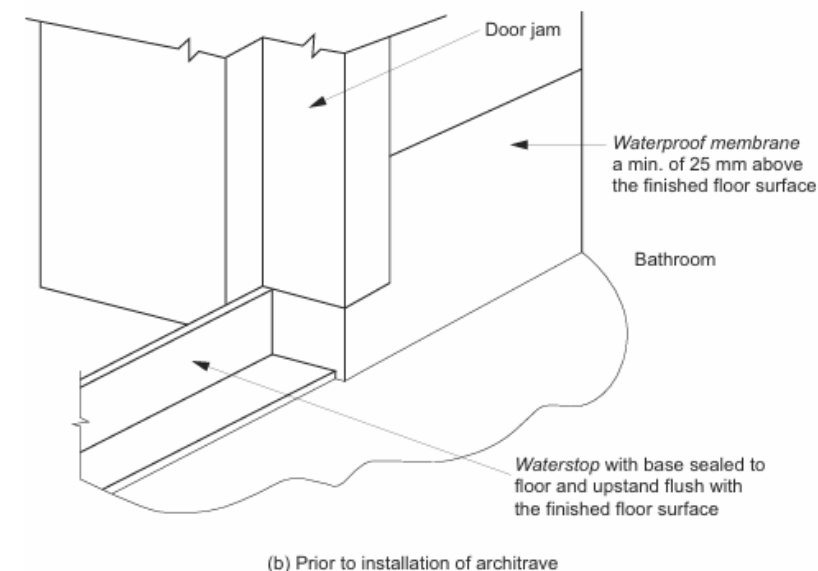

7	28-07-2026	CDC ISSUE	
REV	DATE	DESCRIPTION	BY

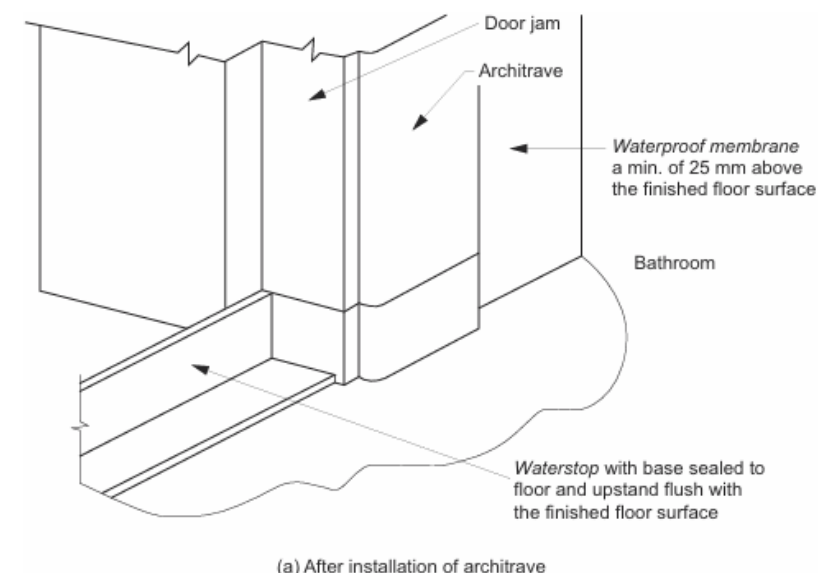

THIS DRAWING IS THE EXCLUSIVE PROPERTY OF THE DEVELOPER & THE REPRODUCTION OF ANY PART WITHOUT THE PRIOR WRITTEN CONSENT OF THE DEVELOPER IS A VIOLATION OF APPLICABLE LAWS. IN NO EVENT SHALL THE DEVELOPER BE HELD RESPONSIBLE FOR ANY SOCIAL, COLLATERAL, INCIDENTAL OR CONSEQUENTIAL LIABILITY IN CONNECTION WITH THE USE OF THIS DIGITAL DATA ONCE RELEASED FROM THE DEVELOPER'S OFFICE. THIS DRAWING IS TO BE READ & UNDERSTOOD IN CONJUNCTION WITH THE STRUCTURAL, MECHANICAL, ELECTRICAL & / OR ANY OTHER CONSULTANT DOCUMENTATION AS MAY BE APPLICABLE TO THE PROJECT PRIOR TO THE START OF ANY WORKS AND FOR ITS DURATION.

PROJECT:
2 GOUNDREY STREET
LOT 70 2 GOUNDREY STREET
CATHERINE FIELDS


DRAWING TITLE:

GENERAL NOTES

NORTH:

LOT NO: 70	DATE: 15-09-2026	SCALE: 1 : 2	DRAWING No: CDC.02B	REV: 7
DRAWN BY: AS	CHECKED BY: RH			ISSUED BY:
DRAFTED BY: SL	CLIENT NAME: Gopal Narayanappa & Shobha Srinivas Reddy			


CDC ISSUE

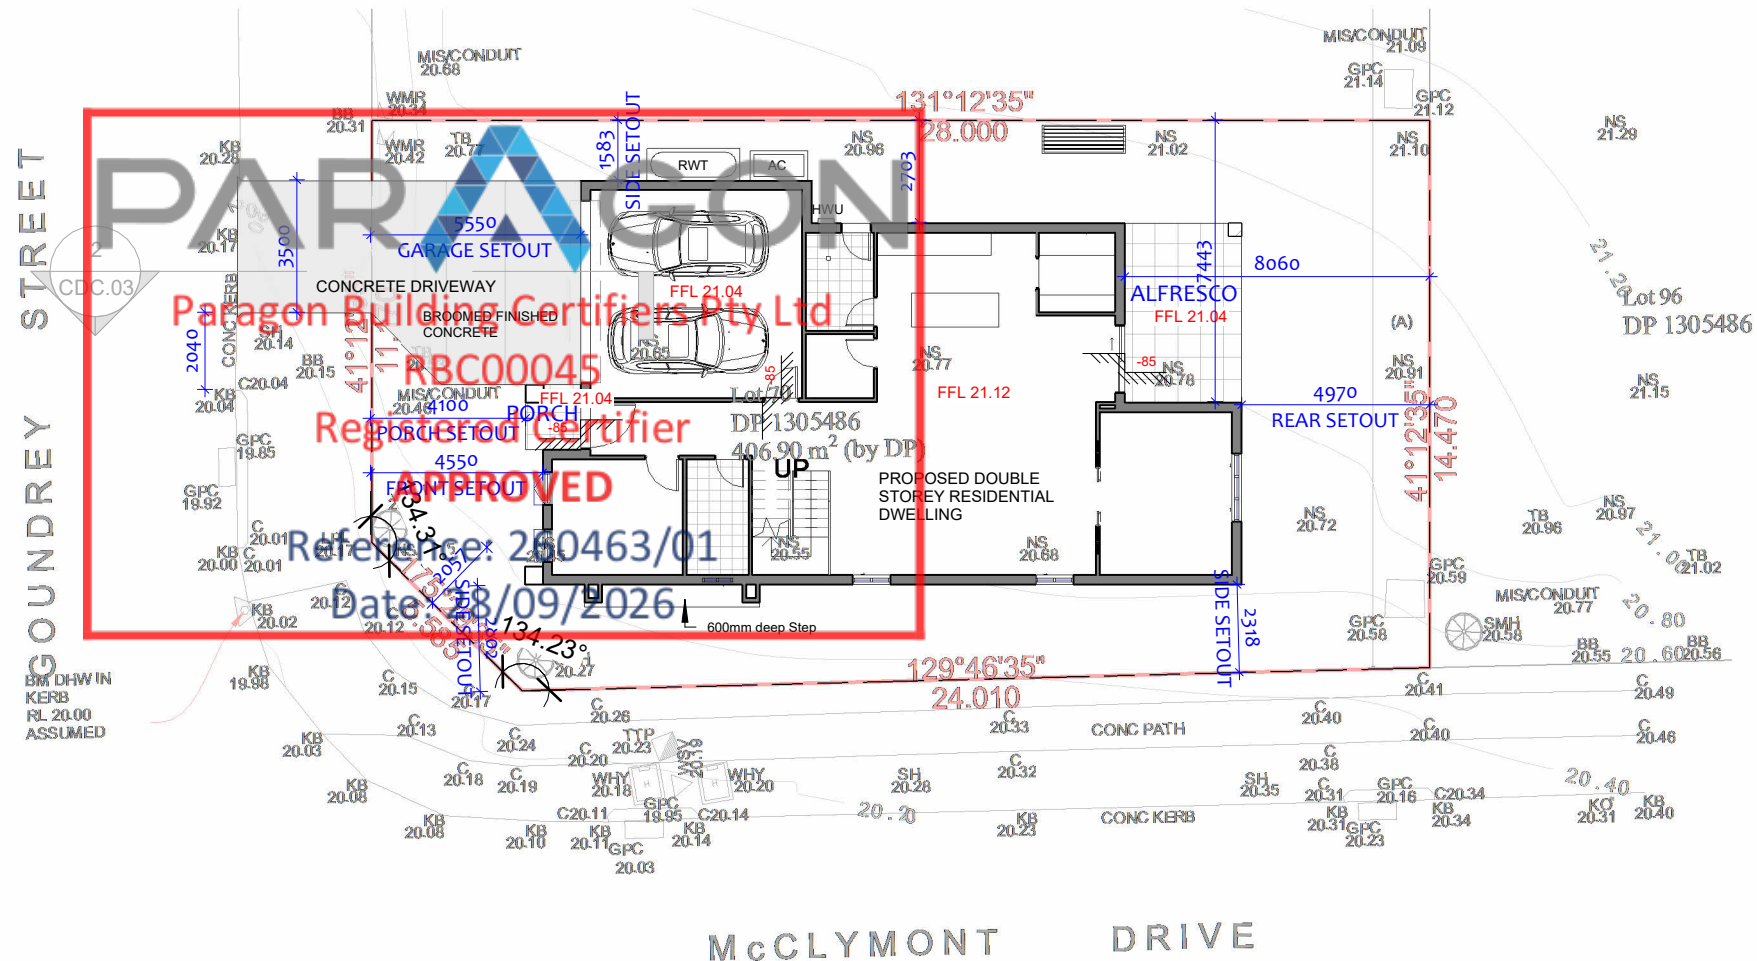

AREA SCHEDULE (RENTABLE)	
NAME	AREA (m2)
LOT AREA	406.9
GROUND FLOOR	118
FIRST FLOOR	120
GARAGE	31
STAIRCASE VOID	6
PRIVATE OPEN SPACE	24
DRIVEWAY	28.3
FRONT LANDSCAPE	87.4
REAR LANDSCAPE	102.9

GREENFIELD HOUSING CODE COMPLIANCE TABLE

DESCRIPTION		COMPLIANCE		COMMENT
ELEMENT	CODE CONTROL	REQUIREMNT	PROPOSED	
LOAND ZONE	1 GENERAL RESIDENTIAL			
LOT NO	LOT 70			
LOT AREA	406.90 m2			
LOT WIDTH	Standard Lot Min. 6m at Building Line facing primary road	6.0m	15 m	YES
HEIGHT	MAX. Height	8.5m	8.3m (MAX.)	YES
FRONT SETBACK	FRONT SET BACK (Min. Setback from Primary Road) For 300-350 sqm. Lot	4.5 m	4.5m	YES
REAR SET BACK (MIN.)	GROUND FLOOR	3m	4.9m	YES
	FIRST FLOOR	6m	8 m	
SIDE SET BACK (MIN.)	GROUND FLOOR	0.9/2m	1.58/2.3m	YES
	FIRST FLOOR	0.9/2m	2.7/2.3m	
FLOOR SPACE RATIO (FSR)	25% of lot area + 150m2	251.725m2	251 m2	YES
GROSS FLOOR AREA PLAN	GROUND FLOOR		118 m2	
	FIRST FLOOR		120 m2	
GARAGE			31m2	
TOTAL FLOOR AREA			251 m2	
ROOF AREA			229 m2	
PRIVATE OPEN SPACE	>10m Lot width	24m2	24 m2	YES
LANDSCAPE AREA	15 % of TOTAL LAND AREA	50.4 m2	190.3 m2	YES

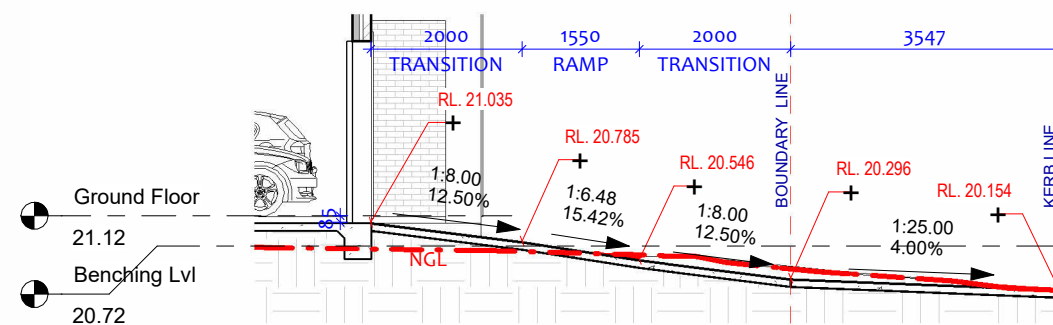

2 DRIVEWAY SECTION
1 : 100

REV	DATE	DESCRIPTION	BY
9	15-09-2026	470x470 feature column added, FW6 shifted towards Secondary facade - Krishna	
8	7-09-2026	Feature columns removed - Ekta	
7	28-07-2026	CDC ISSUE	



THIS DRAWING IS THE EXCLUSIVE PROPERTY OF THE DEVELOPER & THE REPRODUCTION OF ANY PART WITHOUT THE PRIOR WRITTEN CONSENT OF THE DEVELOPER IS A VIOLATION OF APPLICABLE LAWS. IN NO EVENT SHALL THE DEVELOPER BE HELD LIABLE FOR SPECIAL COLLATERAL, INCIDENTAL OR CONSEQUENTIAL LIABILITY IN CONNECTION WITH THE USE OF THIS DIGITAL DATA ONCE RELEASED FROM THE DEVELOPER'S OFFICE. THIS DRAWING IS TO BE READ & UNDERSTOOD IN CONJUNCTION WITH THE STRUCTURAL, MECHANICAL, ELECTRICAL & / OR ANY OTHER CONSULTANT'S DOCUMENTATION AS MAY BE APPLICABLE TO THE PROJECT PRIOR TO THE START OF ANY WORKS AND FOR ITS DURATION.

PROJECT:
2 GOUNDREY STREET
LOT 70 2 GOUNDREY STREET
CATHERINE FIELDS

DRAWING TITLE:
LOCATION PLAN
AND SITE PLAN

NORTH:


LOT NO: 70	DATE: 15-09-2026	SCALE: As indicated	DRAWING No: CDC.03	REV: 9
DRAWN BY: AS	CHECKED BY: RH			
DRAFTED BY: SL	CLIENT NAME: Gopal Narayanappa & Shobha Srinivas Reddy			

CDC ISSUE

BUSHFIRE NOTES:
THE DESIGN SHALL BE MANAGED AS AN INNER PROTECTION AREA (IPA) AS OUTLINED WITHIN SECTION 4.1.3 AND APPENDIX 5 OF "PLANNING FOR BUSHFIRE PROTECTION 2006" AND THE NSW RURAL FIRE SERVICE'S DOCUMENT "STANDARDS FOR ASSET PROTECTION ZONES"

WATERPROOFING WORK TO BE AS PER PART 10.2 OF THE ABCB HOUSING PROVISIONS STANDARD 2022

IMPORTANT NOTES:
ALL DIMENSIONS AND NOTES ON ALL PLANS MUST BE CHECKED AND VERIFIED BY BUILDERS AND OWNER PRIOR TO COMMENCEMENT OF ANY BUILDING WORKS. TO CLARIFY AND CONFIRM WITH CONSTRUCTION COMPANY FOR DISCREPANCIES ON ALL DOCUMENTS AND PLANS PROVIDED FOR CONSTRUCTION. ANY WORK INDICATED ON THE PLAN BUT NOT IN THE SPECIFICATION BUT WHICH IS NECESSARY AS PART OF THE CONTRACT, VARIATION TO PLANS, SPECIFICATIONS MAY NOT BE MADE WITHOUT THE WRITTEN CONSENT OF OWNER. IT IS THE RESPONSIBILITY OF THE BUILDER/END USER TO VERIFY PLANS AND SPECIFICATIONS AS TO THEIR ACCURACY AND COMPLY CURRENT BCA AND AUSTRALIAN STANDARDS. WINDOWS TO COMPLY WITH 3.9.3.5 OF THE BCA.

THE FINISHED ROOM SIZE WILL VARY DEPENDING ON GYPROCK THICKNESS, WALL FINISH I.E TILES AND GLUE, BEDDING HEIGHTS, SKIRTING INSTALLATION.

THE MEASUREMENTS GIVEN IS STRUCTURAL SIZES ONLY NOT FINISHED FLOOR SIZE.



1 Ground Floor

1 : 100

FALL TO THE FLOOR WASTE TO BE MIN. 1:80 AND MAX. 1:50

NOTE: PLEASE REFER TO TENDER FOR ALL INCLUSIONS.

9	15-09-2026	470x470 feature column added, FW6 shifted towards Secondary facade - Krishna	
8	7-09-2026	Feature columns removed - Ekta	
7	28-07-2026	CDC ISSUE	
6	16-07-2026	2 Awning Windows each to the Front on both floors, 2 double height rendered columns and horizontal connection on the Secondary Street side - Ekta.	
REV	DATE	DESCRIPTION	BY

THIS DRAWING IS THE EXCLUSIVE PROPERTY OF THE DEVELOPER & THE REPRODUCTION OF ANY PART WITHOUT THE PRIOR WRITTEN CONSENT OF THE DEVELOPER IS A VIOLATION OF APPLICABLE LAWS. IN NO EVENT SHALL THE DEVELOPER BE HELD LIABLE FOR SPECIAL COLLATERAL, INCIDENTAL OR CONSEQUENTIAL LIABILITY IN CONNECTION WITH THE USE OF THIS DIGITAL DATA ONCE RELEASED FROM THE DEVELOPER'S OFFICE. THIS DRAWING IS TO BE READ & UNDERSTOOD IN CONJUNCTION WITH THE STRUCTURAL, MECHANICAL, ELECTRICAL & / OR ANY OTHER CONSULTANT'S DOCUMENTATION AS MAY BE APPLICABLE TO THE PROJECT PRIOR TO THE START OF ANY WORKS AND FOR ITS DURATION.

PROJECT:
2 GOUNDREY STREET

LOT 70 2 GOUNDREY STREET
CATHERINE FIELDS

DRAWING TITLE:
GROUND FLOOR PLAN

NORTH:

LOT NO: 70	DATE: 15-09-2026	SCALE: 1 : 100	DRAWING No: CDC.05	REV: 9
DRAWN BY: AS	CHECKED BY: RH			ISSUED BY:
DRAFTED BY: SL	CLIENT NAME: Gopal Narayanappa & Shobha Srinivas Reddy			

CDC ISSUE

BUSHFIRE NOTES:


THE DESIGN SHALL BE MANAGED AS AN INNER PROTECTION AREA (IPA) AS OUTLINED WITHIN SECTION 4.1.3 AND APPENDIX 5 OF "PLANNING FOR BUSHFIRE PROTECTION 2006" AND THE NSW RURAL FIRE SERVICE'S DOCUMENT "STANDARDS FOR ASSET PROTECTION ZONES"

WATERPROOFING WORK TO BE AS PER PART 10.2 OF THE ABCB HOUSING PROVISIONS STANDARD 2022

IMPORTANT NOTES:
ALL DIMENSIONS AND NOTES ON ALL PLANS MUST BE CHECKED AND VERIFIED BY BUILDERS AND OWNER PRIOR TO COMMENCEMENT OF ANY BUILDING WORKS. TO CLARIFY AND CONFIRM WITH CONSTRUCTION COMPANY FOR DISCREPANCIES ON ALL DOCUMENTS AND PLANS PROVIDED FOR CONSTRUCTION. ANY WORK INDICATED ON THE PLAN BUT NOT IN THE SPECIFICATION BUT WHICH IS NECESSARY AS PART OF THE CONTRACT, VARIATION TO PLANS, SPECIFICATIONS MAY NOT BE MADE WITHOUT THE WRITTEN CONSENT OF OWNER. IT IS THE RESPONSIBILITY OF THE BUILDER/END USER TO VERIFY PLANS AND SPECIFICATIONS AS TO THEIR ACCURACY AND COMPLY CURRENT BCA AND AUSTRALIAN STANDARDS. WINDOWS TO COMPLY WITH 3.9.3.5 OF THE BCA.

THE FINISHED ROOM SIZE WILL VARY DEPENDING ON GYPROCK THICKNESS, WALL FINISH I.E TILES AND GLUE, BEDDING HEIGHTS, SKIRTING INSTALLATION.

THE MEASUREMENTS GIVEN IS STRUCTURAL SIZES ONLY NOT FINISHED FLOOR SIZE.

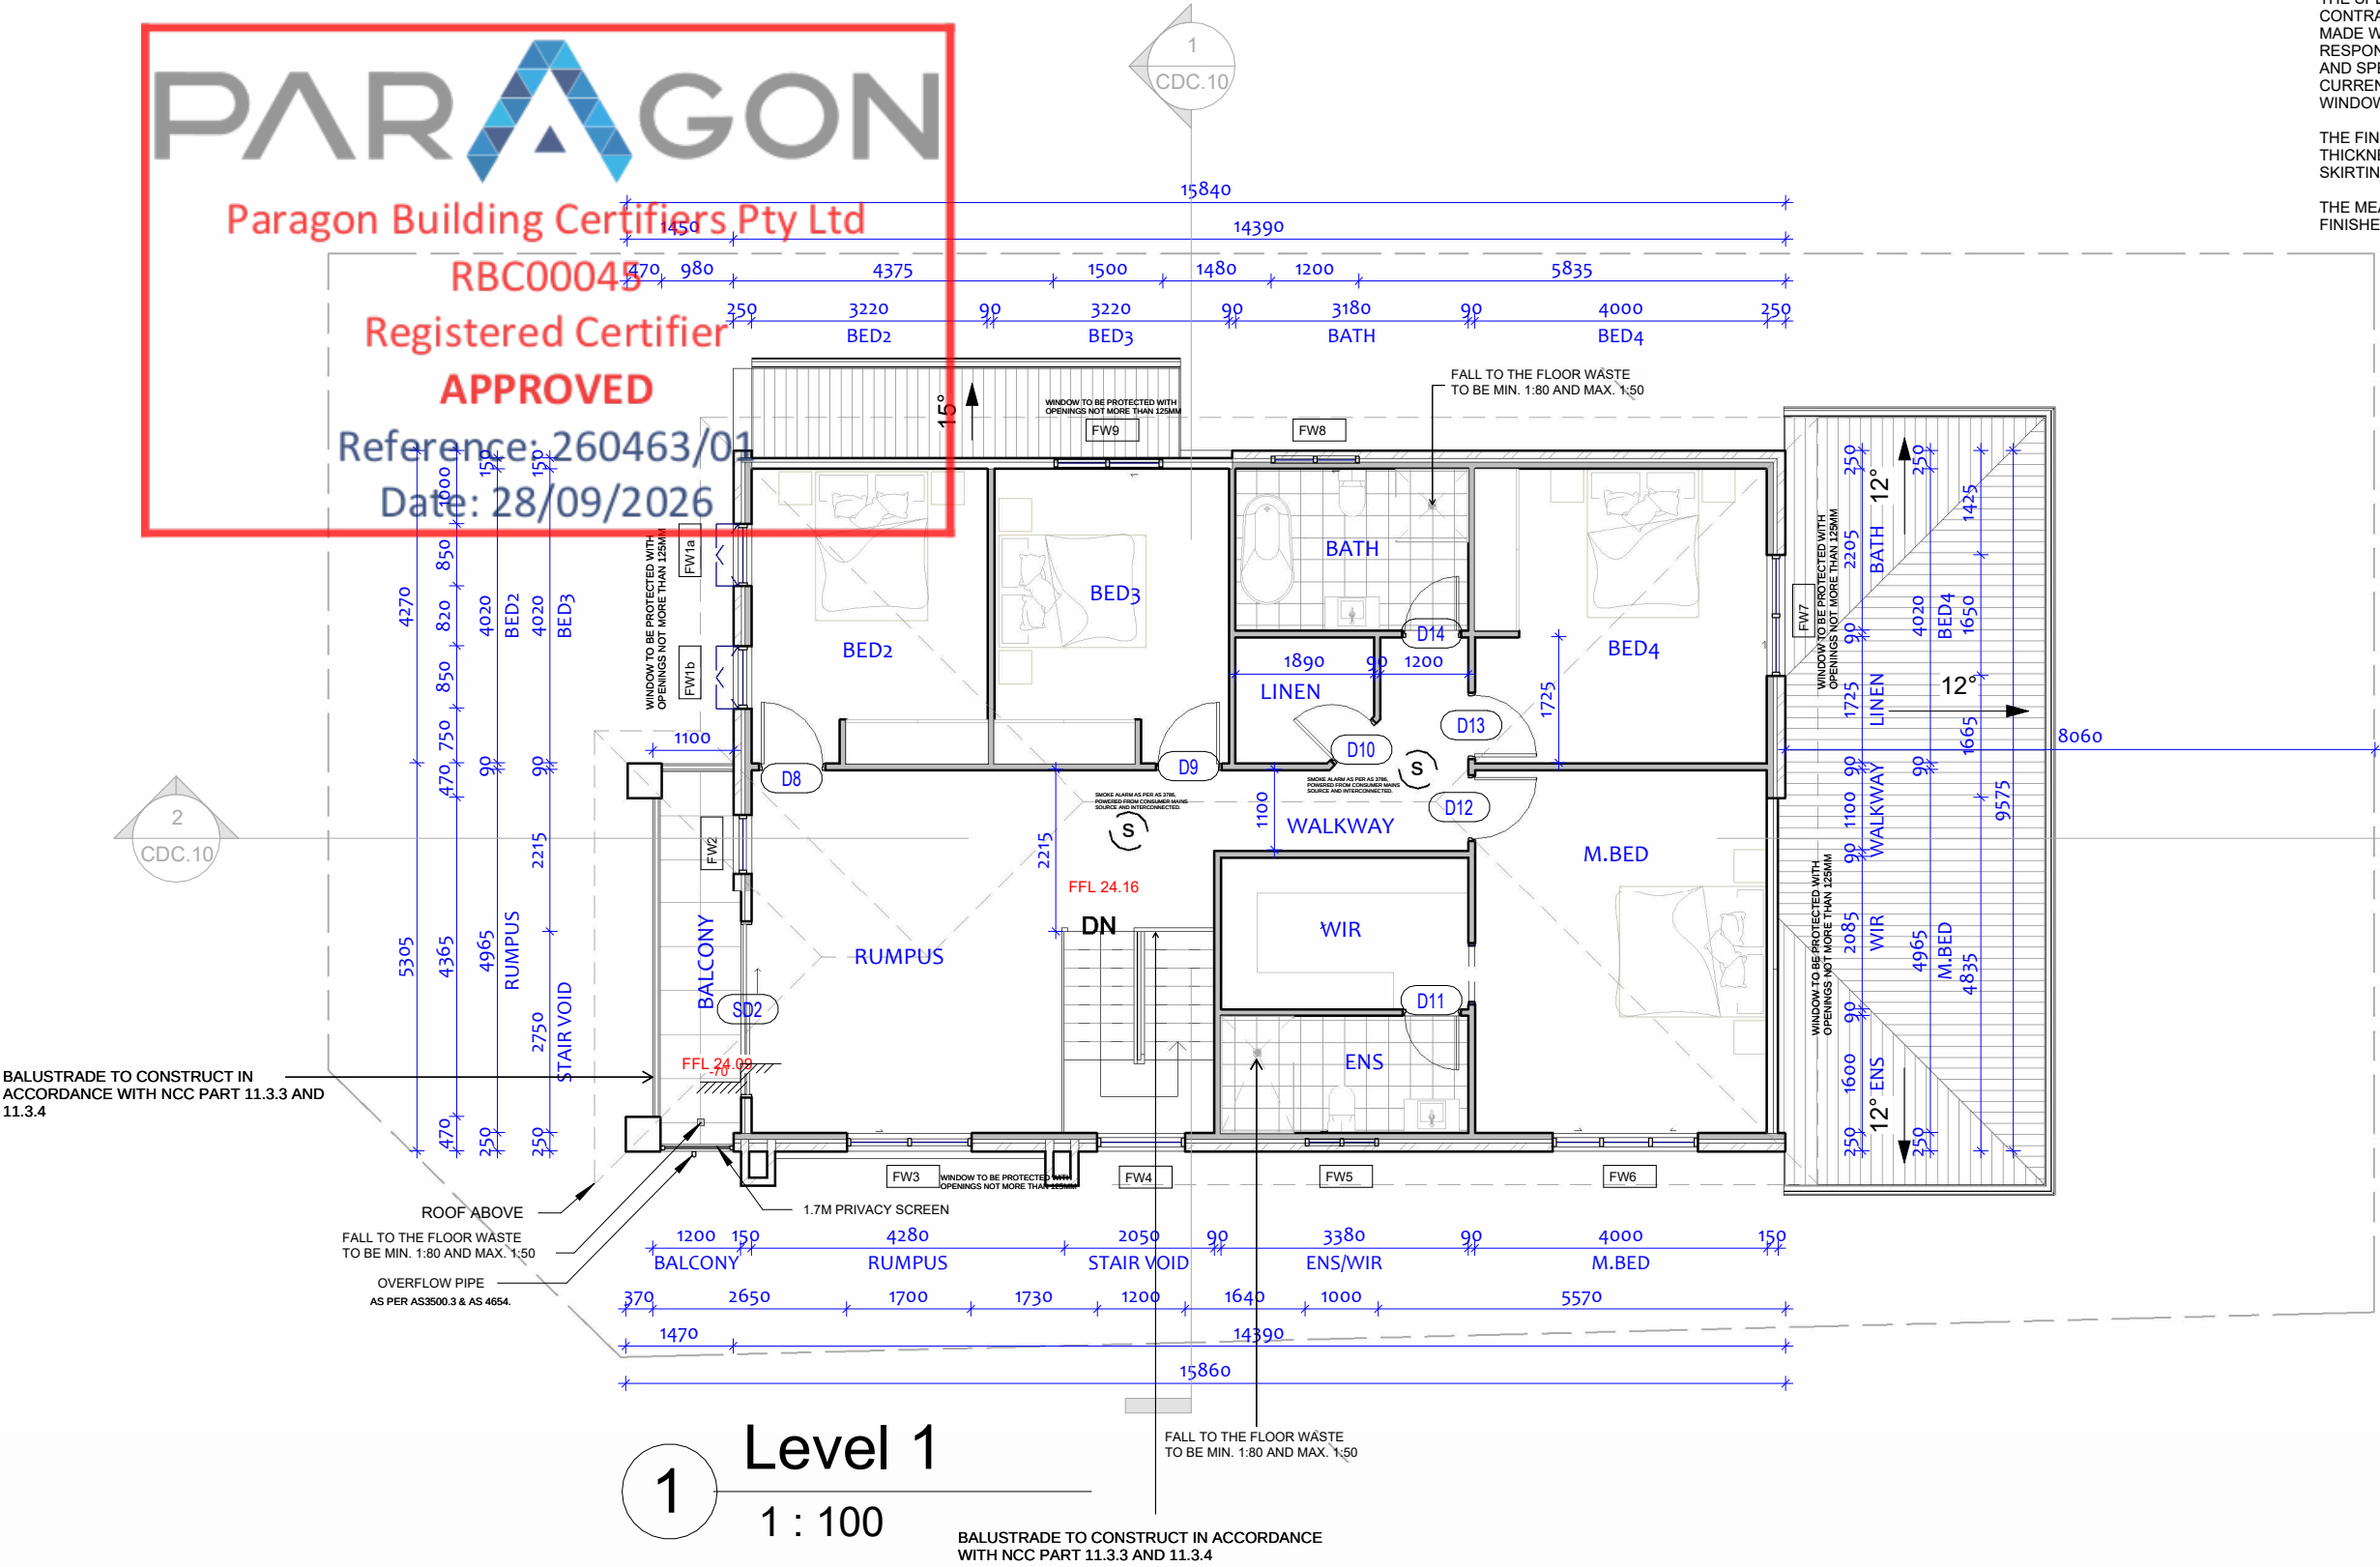

NOTE: PLEASE REFER TO TENDER FOR ALL INCLUSIONS.

REV	DATE	DESCRIPTION	BY
9	15-09-2026	470x470 feature column added, FW6 shifted towards Secondary facade - Krishna	
7	28-07-2026	CDC ISSUE	
6	16-07-2026	2 Awning Windows each to the Front on both floors, 2 double height rendered columns and horizontal connection on the Secondary Street side - Ekta.	



THIS DRAWING IS THE EXCLUSIVE PROPERTY OF THE DEVELOPER & THE REPRODUCTION OF ANY PART WITHOUT THE PRIOR WRITTEN CONSENT OF THE DEVELOPER IS A VIOLATION OF APPLICABLE LAWS. IN NO EVENT SHALL THE DEVELOPER BE HELD LIABLE FOR SPECIAL COLLATERAL, INCIDENTAL OR CONSEQUENTIAL LIABILITY IN CONNECTION WITH THE USE OF THIS DIGITAL DATA ONCE RELEASED FROM THE DEVELOPER'S OFFICE. THIS DRAWING IS TO BE READ & UNDERSTOOD IN CONJUNCTION WITH THE STRUCTURAL, MECHANICAL, ELECTRICAL & / OR ANY OTHER CONSULTANT'S DOCUMENTATION AS MAY BE APPLICABLE TO THE PROJECT PRIOR TO THE START OF ANY WORKS AND FOR ITS DURATION.

PROJECT:
2 GOUNDREY STREET

LOT 70 2 GOUNDREY STREET
CATHERINE FIELDS


DRAWING TITLE:
**FIRST FLOOR
LEVEL**

NORTH:


LOT NO:	DATE:	SCALE:	DRAWING No:	REV:
70	15-09-2026	1 : 100	CDC.06	9
DRAWN BY:	CHECKED BY:			ISSUED BY:
AS	RH			
DRAFTED BY:	CLIENT NAME:			
SL	Gopal Narayanappa & Shobha Srinivas Reddy			

CDC ISSUE

THE DESIGN SHALL BE MANAGED AS AN INNER PROTECTION AREA (IPA) AS OUTLINED WITHIN SECTION 4.1.3 AND APPENDIX 5 OF "PLANNING FOR BUSHFIRE PROTECTION 2006" AND THE NSW RURAL FIRE SERVICE'S DOCUMENT "STANDARDS FOR ASSET PROTECTION ZONES"

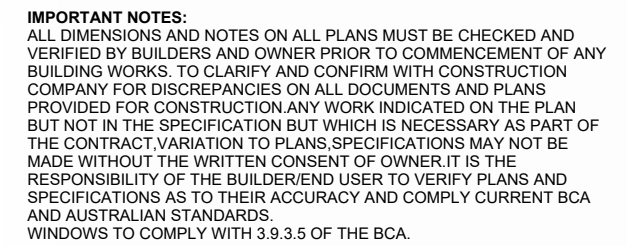

1. IN CLIMATE ZONES 6,7 AND 8, A ROOF MUST HAVE A ROOF SPACE THAT (A) IS LOCATED

- (I) IMMEDIATELY ABOVE THE *PRIMARY INSULATION LAYER*, OR
- (II) IMMEDIATELY ABOVE SARKING WITH A *VAPOUR PERMEANCE* OF NOT LESS THAN 1.14 $\mu\text{g}/\text{N}\cdot\text{S}$, WHICH IS IMMEDIATELY ABOVE THE *PRIMARY INSULATION LAYER*, OR
- (III) IMMEDIATELY ABOVE CEILING INSULATION THAT MEETS THE REQUIREMENTS OF 13.2.3(3) AND 13.2.3(4); AND

(B) HAS A HEIGHT OF NOT LESS THAN 20MM; AND

(C) IS EITHER -

- (I) VENTILATED TO OUTDOOR AIR THROUGH EVENLY DISTRIBUTED OPENINGS IN ACCORDANCE WITH TABLE 10.8.3; OR
- (II) LOCATED IMMEDIATELY UNDERNEATH THE ROOF TILES OF A UNSARKED TILED ROOF.



Roof Schedule			
Mark	Base Level	Area	Comments
R3	Level 1	7 m²	COLORBOND
R2	Level 1	38 m²	COLORBOND
R1	CEILING LEVEL	186 m²	COLORBOND
Grand total: 3		232 m²	





RUBY
H O M E S

THIS DRAWING IS THE EXCLUSIVE PROPERTY OF THE DEVELOPER & THE REPRODUCTION OF ANY PART WITHOUT THE PRIOR WRITTEN CONSENT OF THE DEVELOPER IS A VIOLATION OF APPLICABLE LAWS. IN NO EVENT SHALL THE DEVELOPER BE HELD LIABLE FOR SPECIAL, COLLATERAL, INCIDENTAL OR CONSEQUENTIAL LIABILITY IN CONNECTION WITH THE USE OF THIS DIGITAL DATA ONCE RELEASED FROM THE DEVELOPER'S OFFICE. THIS DRAWING IS TO BE READ & UNDERSTOOD IN CONJUNCTION WITH THE STRUCTURAL, MECHANICAL, ELECTRICAL & / OR ANY OTHER CONSULTANT DOCUMENTATION AS MAY BE APPLICABLE TO THE PROJECT PRIOR TO THE START OF ANY WORKS AND FOR.

NORTH:

A circular compass rose with a thick black line pointing towards the top-left, indicating North.

LOT NO: 70	DATE: 15-09-2026	SCALE: 1 : 100	DRAWING No:	REV: 9
DRAWN BY: AS	CHECKED BY: RH		CDC.07	ISSUED BY:
DRAFTED BY: SL	CLIENT NAME: Gopal Narayanappa & Shobha Srinivas Reddy			

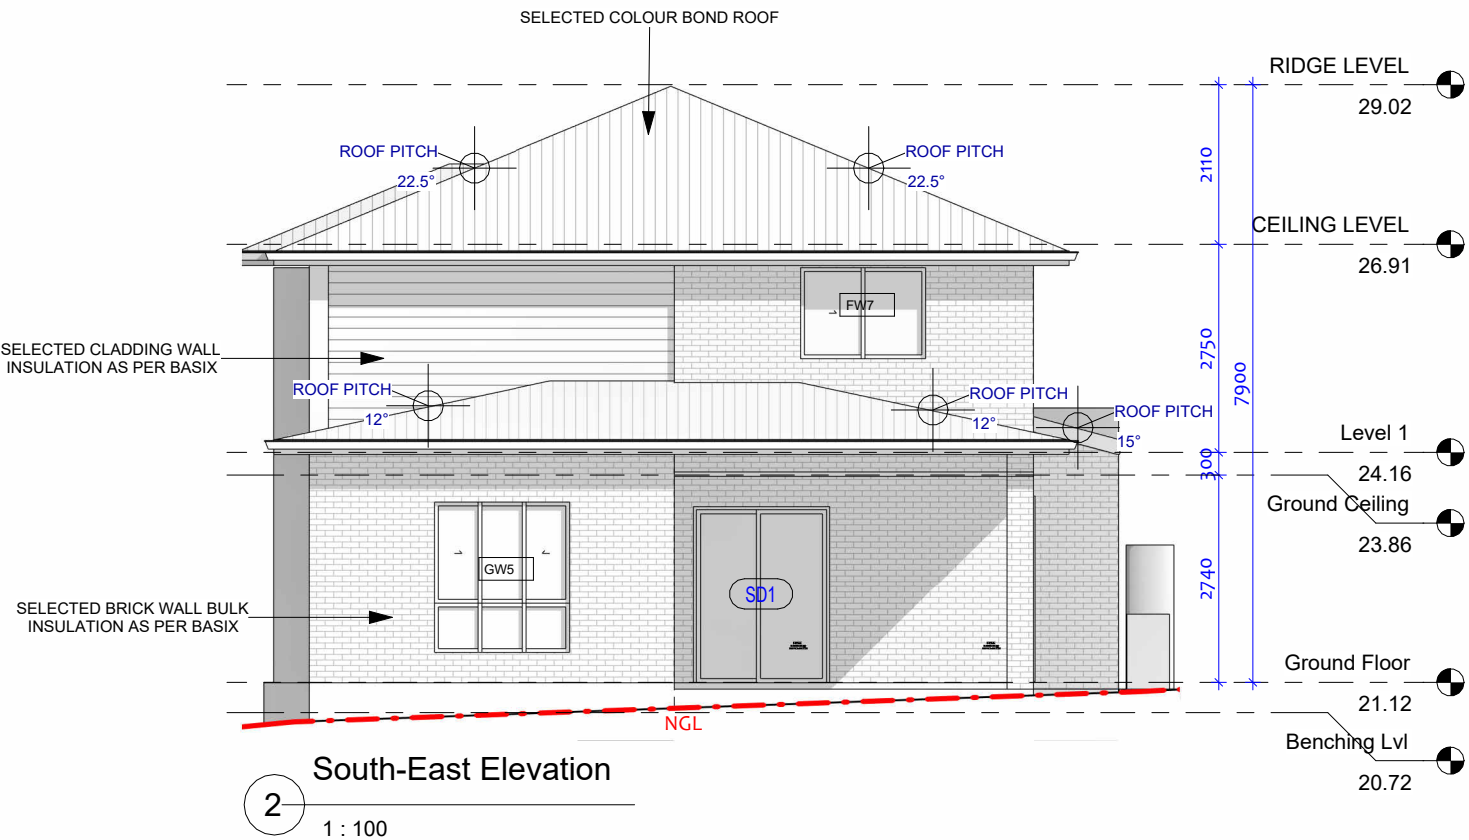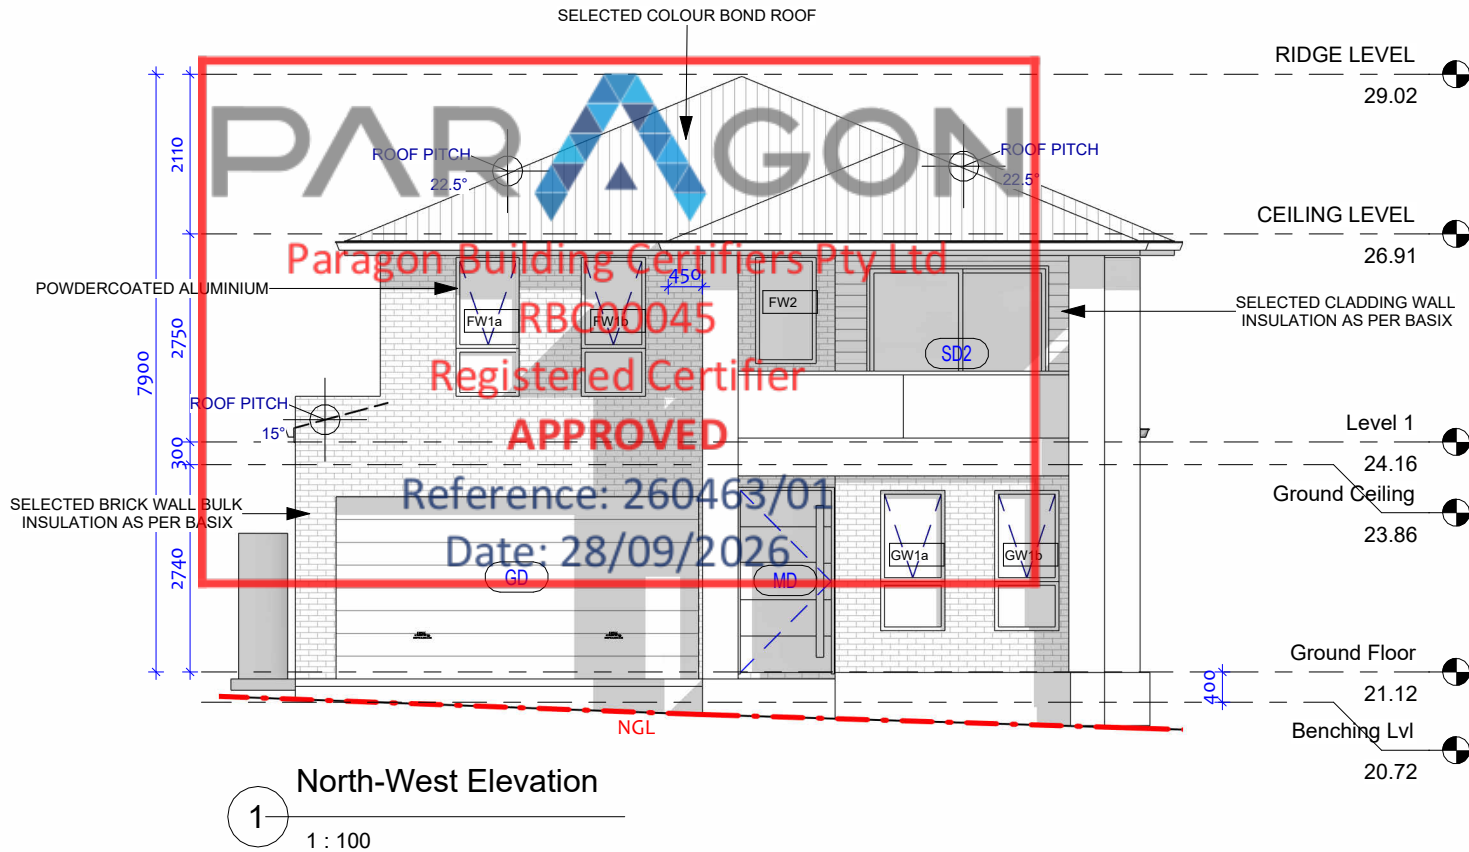

Window Schedule 1					
Mark	Height	Width	Sill Height	Head Height	Description

Ground Floor

GW1a	1850	850	550	2400	AWNING
GW1b	1850	850	550	2400	AWNING
GW2	500	800	1900	2400	SLIDING
GW3	1400	1000	1000	2400	SLIDING
GW4	1400	1000	1000	2400	SLIDING
GW5	2000	1800	400	2400	SLIDING & FIXED
GW6	600	1200	950	1550	SLIDING
GW7	600	1800	950	1550	FIXED

Ground Floor: 8

Level 1

FW1a	1850	850	600	2450	AWNING
FW1b	1850	850	600	2450	AWNING
FW2	1400	800	1050	2450	FIXED
FW3	1400	1700	1050	2450	SLIDING
FW4	2050	1200	400	2450	FIXED
FW5	600	1000	1850	2450	SLIDING
FW6	1200	2000	1250	2450	SLIDING & FIXED
FW7	1200	1650	1250	2450	SLIDING
FW8	800	1200	1650	2450	SLIDING
FW9	800	1500	1650	2450	SLIDING

Level 1: 10

Door Schedule 1				
Mark	Height	Width	Count	Description

Ground Floor

D1	2340	820	1	FLUSH DOOR
D2	2340	720	1	FLUSH DOOR
D3	2340	820	1	FLUSH DOOR
D4	2340	720	1	FLUSH DOOR
D5	2340	720	1	FLUSH DOOR
D6	2340	720	1	FLUSH DOOR
D7	2340	1500	1	FLUSH DOOR
GD	2400	4800	1	GARAGE DOOR
MD	2400	1200	1	SOLID CORE DOOR
SD1	2300	1800	1	SLIDING DOOR

Ground Floor: 10

Level 1

D8	2340	820	1	FLUSH DOOR
D9	2340	820	1	FLUSH DOOR
D10	2340	720	1	FLUSH DOOR
D11	2340	720	1	FLUSH DOOR
D12	2340	820	1	FLUSH DOOR
D13	2340	820	1	FLUSH DOOR
D14	2340	720	1	FLUSH DOOR
SD2	2300	2400	1	SLIDING DOOR

Level 1: 8

CDC ISSUE

				CDC ISSUE	
7	28-07-2026	CDC ISSUE		LOT NO: 70	DATE: 15-09-2026
6	16-07-2026	2 Awning Windows each to the Front on both floors, 2 double height rendered columns and horizontal connection on the Secondary Street side - Ekta.		DRAWN BY: AS	CHECKED BY: RH
REV	DATE	DESCRIPTION	BY	DRAFTED BY: SL	CLIENT NAME: Gopal Narayanappa & Shobha Srinivas Reddy



THIS DRAWING IS THE EXCLUSIVE PROPERTY OF THE DEVELOPER & THE REPRODUCTION OF ANY PART WITHOUT THE PRIOR WRITTEN CONSENT OF THE DEVELOPER IS A VIOLATION OF APPLICABLE LAWS. IN NO EVENT SHALL THE DEVELOPER BE HELD LIABLE FOR SPECIAL COLLATERAL, INCIDENTAL OR CONSEQUENTIAL LIABILITY IN CONNECTION WITH THE USE OF THIS DIGITAL DATA ONCE RELEASED FROM THE DEVELOPER'S OFFICE. THIS DRAWING IS TO BE READ & UNDERSTOOD IN CONJUNCTION WITH THE STRUCTURAL, MECHANICAL, ELECTRICAL & / OR ANY OTHER CONSULTANT'S DOCUMENTATION AS MAY BE APPLICABLE TO THE PROJECT PRIOR TO THE START OF ANY WORKS AND FOR ITS DURATION.

PROJECT:
2 GOUNDREY STREET



LOT 70 2 GOUNDREY STREET
CATHERINE FIELDS

DRAWING TITLE:
ELEVATION 01

NORTH:

DRAWING No: 7
REV: 7
ISSUED BY:

CDC.08

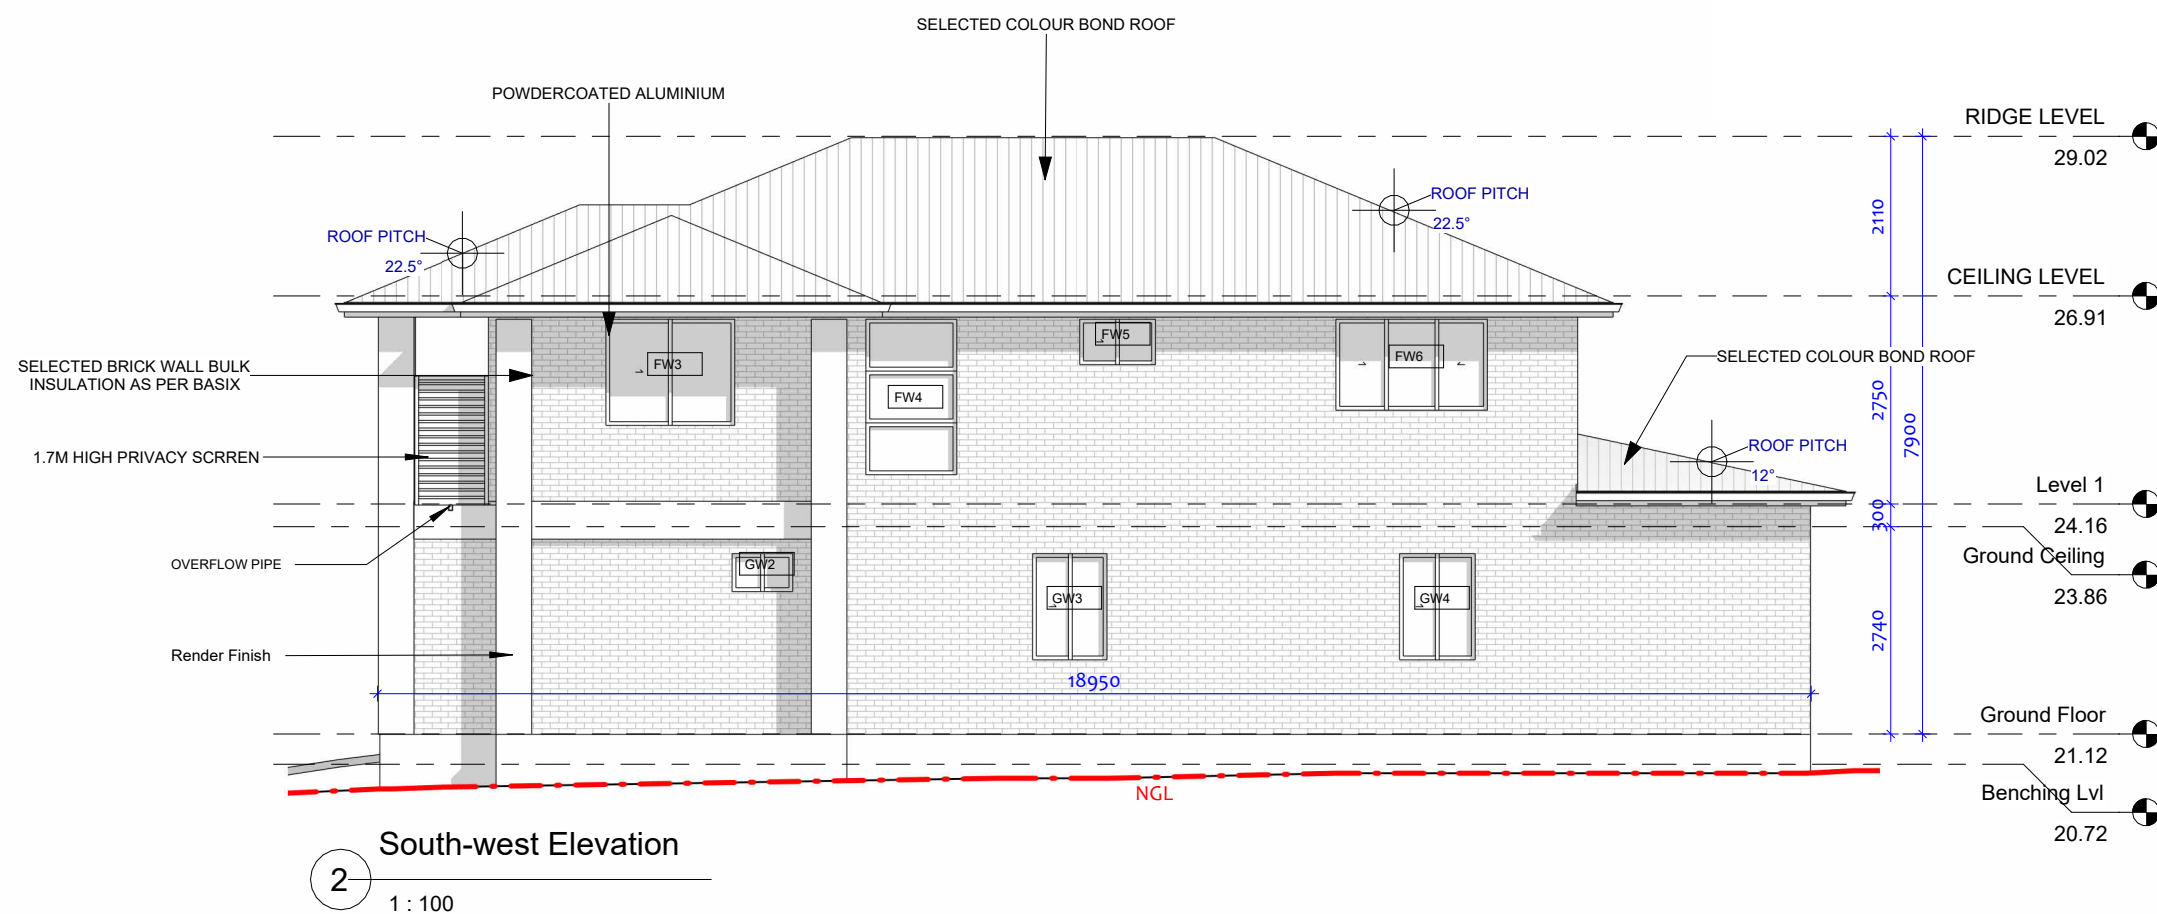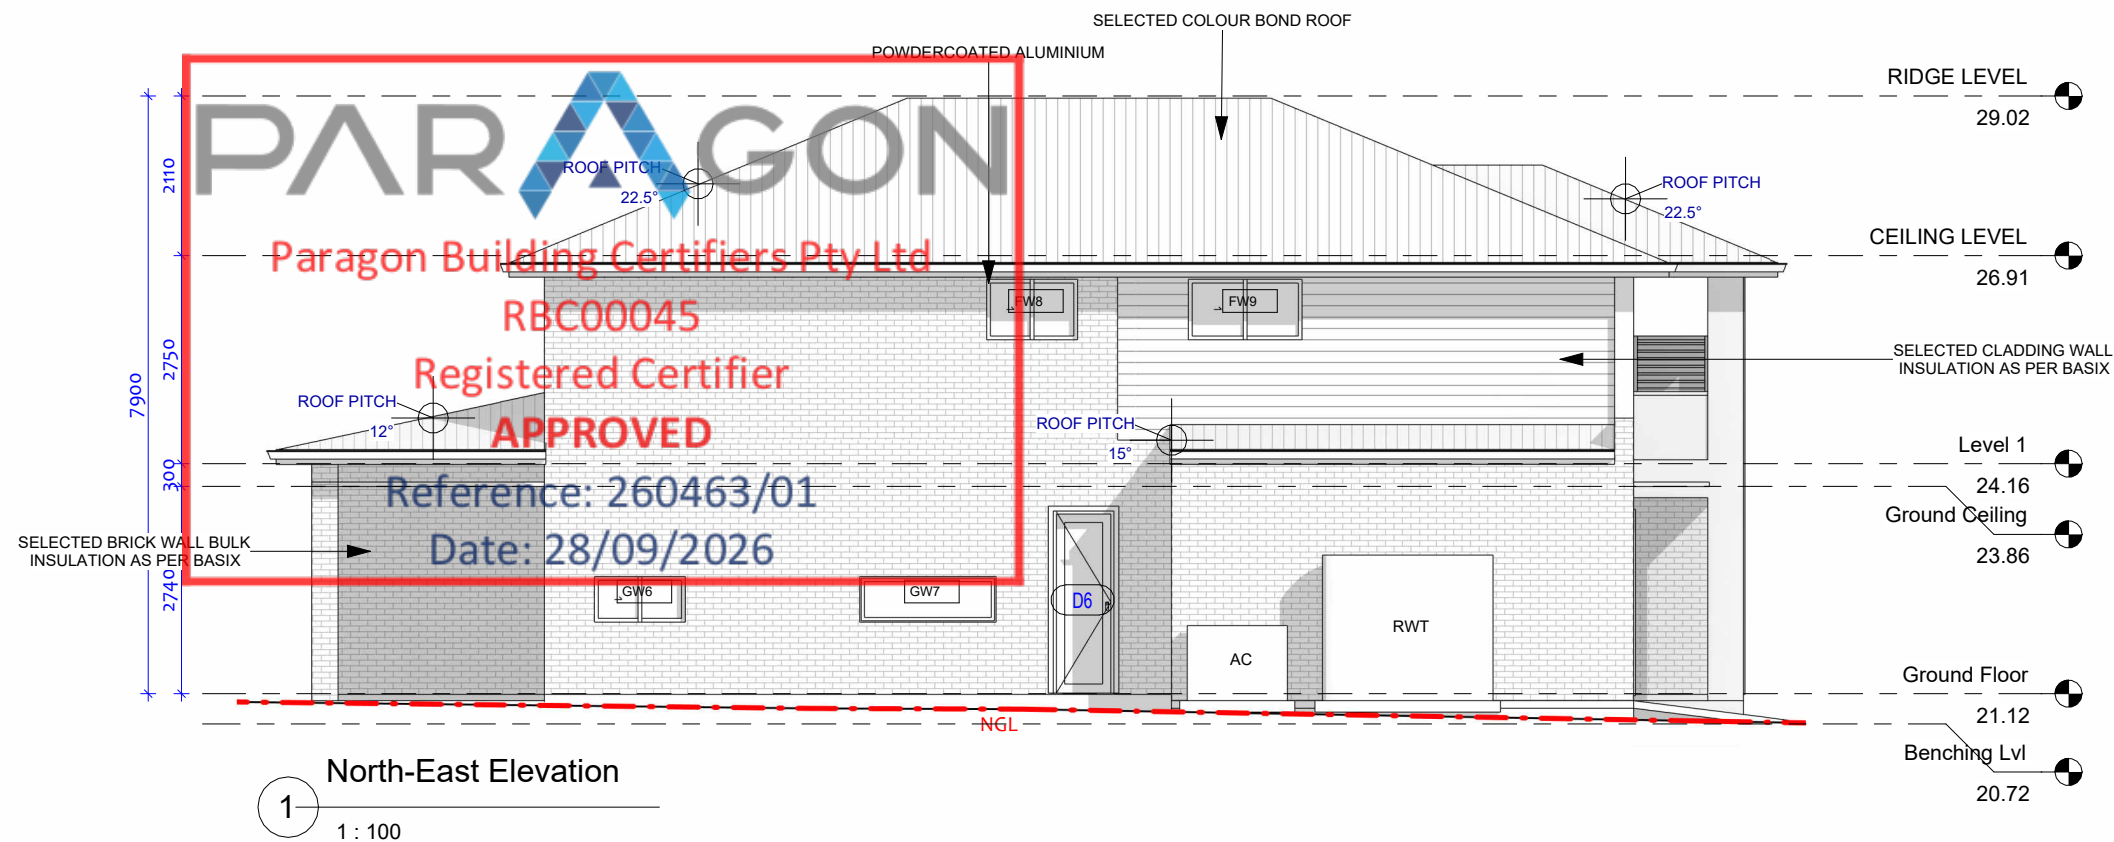

				CDC ISSUE			
9	15-09-2026	470x470 feature column added, FW6 shifted towards Secondary facade - Krishna		LOT NO:	DATE:	SCALE:	DRAWING No:
7	28-07-2026	CDC ISSUE		70	15-09-2026	1 : 100	REV: 9
6	16-07-2026	2 Awning Windows each to the Front on both floors, 2 double height rendered columns and horizontal connection on the Secondary Street side - Ekta.		DRAWN BY:	CHECKED BY:		CDC.09
AS	RH			DRAFTED BY:	CLIENT NAME:		
SL	Gopal Narayanappa & Shobha Srinivas Reddy						
REV	DATE	DESCRIPTION	BY				




THIS DRAWING IS THE EXCLUSIVE PROPERTY OF THE DEVELOPER & THE REPRODUCTION OF ANY PART WITHOUT THE PRIOR WRITTEN CONSENT OF THE DEVELOPER IS A VIOLATION OF APPLICABLE LAWS. IN NO EVENT SHALL THE DEVELOPER BE HELD LIABLE FOR SPECIAL COLLATERAL, INCIDENTAL OR CONSEQUENTIAL LIABILITY IN CONNECTION WITH THE USE OF THIS DIGITAL DATA ONCE RELEASED FROM THE DEVELOPER'S OFFICE. THIS DRAWING IS TO BE READ & UNDERSTOOD IN CONJUNCTION WITH THE STRUCTURAL, MECHANICAL, ELECTRICAL & / OR ANY OTHER CONSULTANT'S DOCUMENTATION AS MAY BE APPLICABLE TO THE PROJECT PRIOR TO THE START OF ANY WORKS AND FOR ITS DURATION.

PROJECT:
2 GOUNDREY STREET


LOT 70 2 GOUNDREY STREET
CATHERINE FIELDS

DRAWING TITLE:
ELEVATION 02

NORTH:

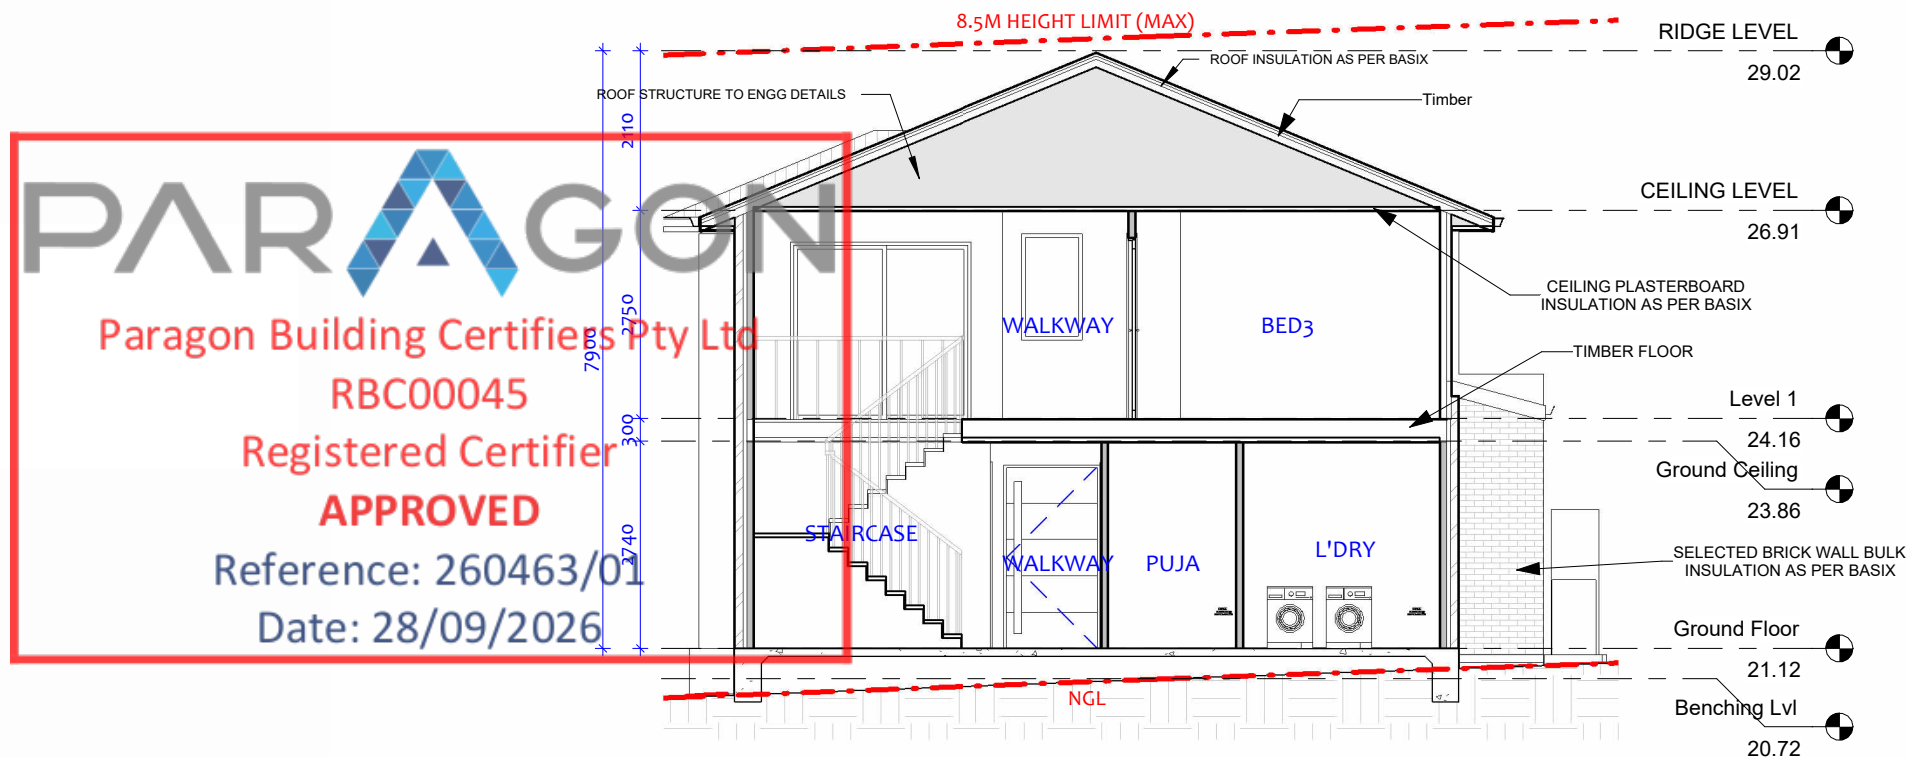

1 CROSS SECTION
1 : 100

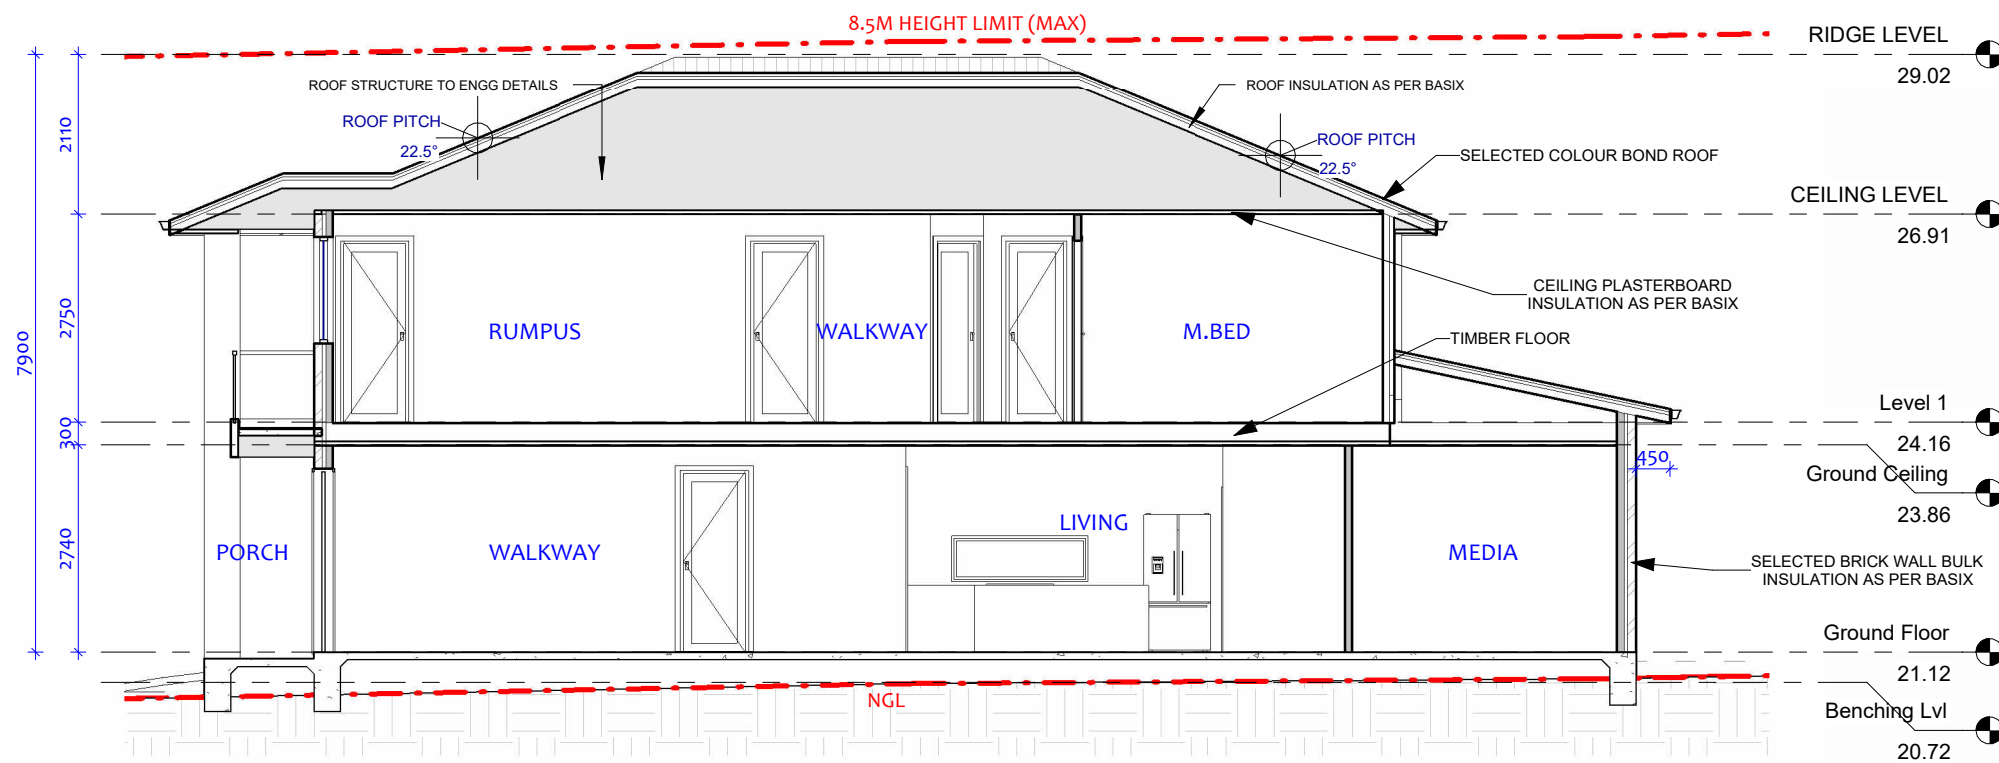

2 LONGITUDINAL SECTION
1 : 100

REV	DATE	DESCRIPTION	BY
7	28-07-2026	CDC ISSUE	

RUBY HOMES

THIS DRAWING IS THE EXCLUSIVE PROPERTY OF THE DEVELOPER & THE REPRODUCTION OF ANY PART WITHOUT THE PRIOR WRITTEN CONSENT OF THE DEVELOPER IS A VIOLATION OF APPLICABLE LAWS. IN NO EVENT SHALL THE DEVELOPER BE HELD LIABLE FOR SPECIAL COLLATERAL, INCIDENTAL OR CONSEQUENTIAL LIABILITY IN CONNECTION WITH THE USE OF THIS DIGITAL DATA ONCE RELEASED FROM THE DEVELOPER'S OFFICE. THIS DRAWING IS TO BE READ & UNDERSTOOD IN CONJUNCTION WITH THE STRUCTURAL, MECHANICAL, ELECTRICAL & / OR ANY OTHER CONSULTANT'S DOCUMENTATION AS MAY BE APPLICABLE TO THE PROJECT PRIOR TO THE START OF ANY WORKS AND FOR ITS DURATION.


PROJECT:
2 GOUNDREY STREET
LOT 70 2 GOUNDREY STREET
CATHERINE FIELDS

DRAWING TITLE:
SECTIONS

NORTH:

LOT NO: 70	DATE: 15-09-2026	SCALE: 1 : 100	DRAWING No: CDC.10	REV: 7
DRAWN BY: AS	CHECKED BY: RH			ISSUED BY:
DRAFTED BY: SL	CLIENT NAME: Gopal Narayanappa & Shobha Srinivas Reddy			


CDC ISSUE

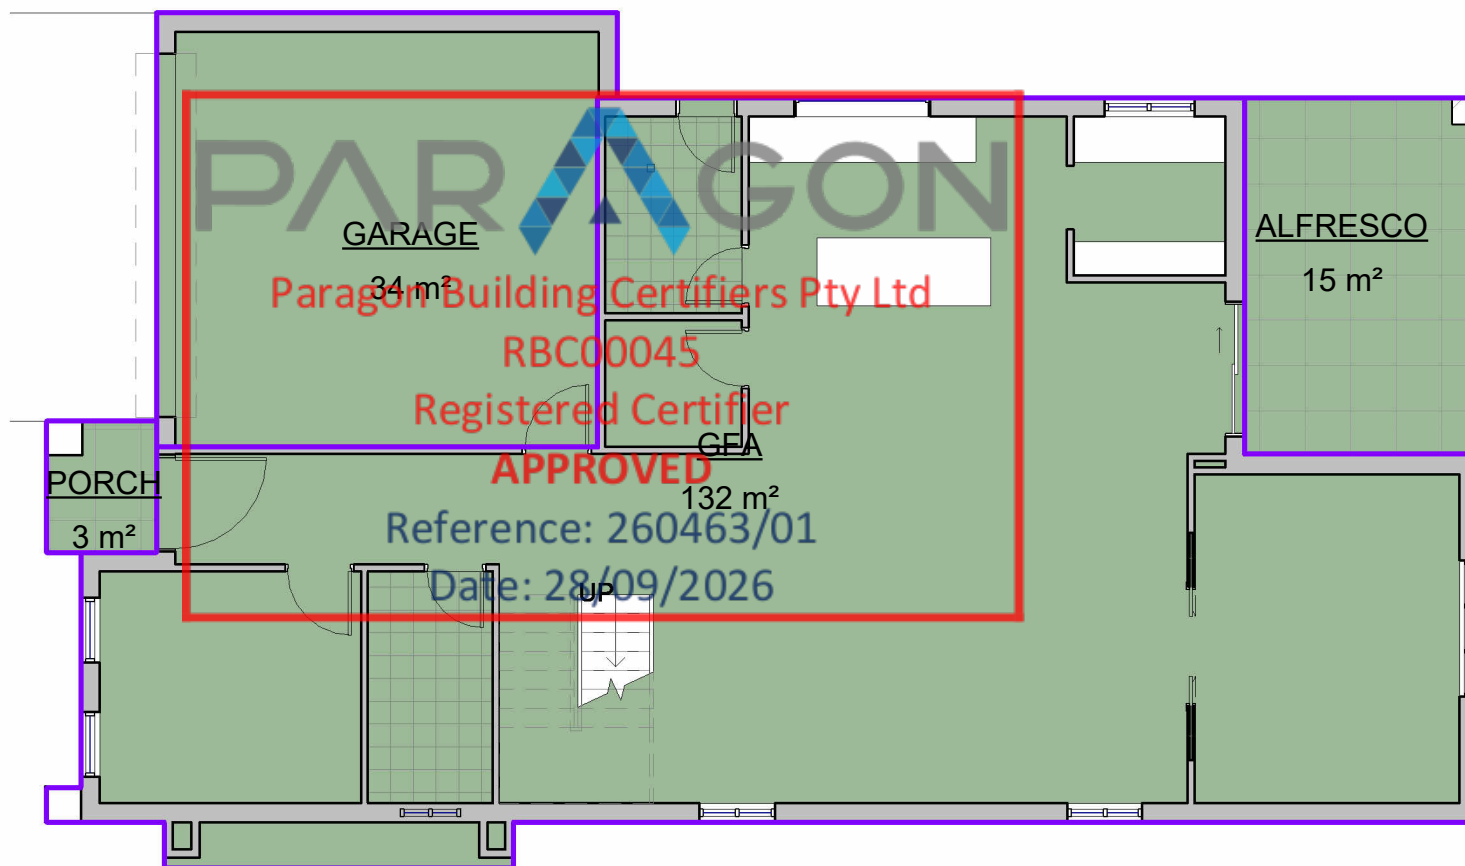

1 Ground Floor
1 : 100

Area Schedule (Gross Building)	
Name	Area

Ground Floor	
GARAGE	34 m ²
GFA	132 m ²
ALFRESCO	15 m ²
PORCH	3 m ²
Ground Floor: 4	183 m ²
Level 1	
FFA	132 m ²
BALCONY	6 m ²
STAIRCASE	6 m ²
Level 1: 3	144 m ²
Grand total: 7	327 m ²

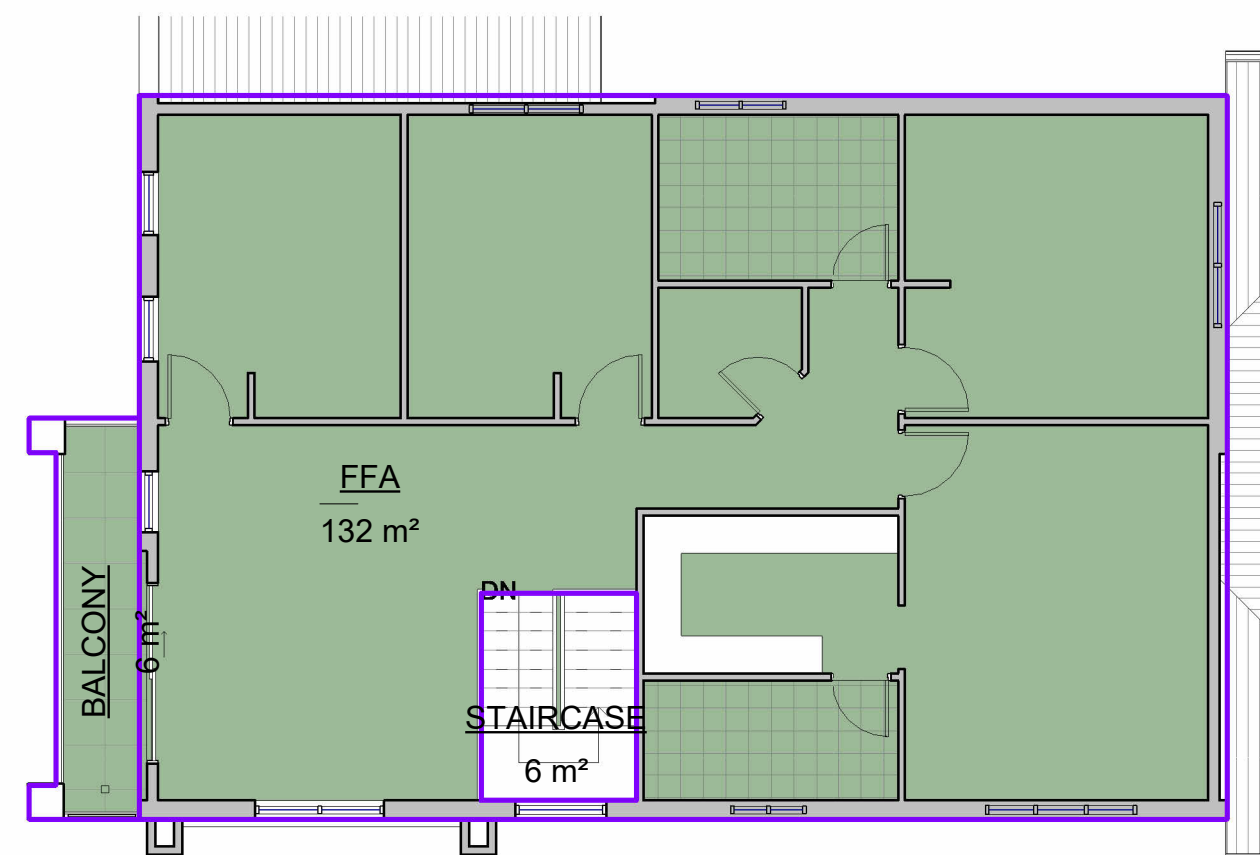

2 Level 1
1 : 100

REV	DATE	DESCRIPTION	BY
7	28-07-2026	CDC ISSUE	
6	16-07-2026	2 Awning Windows each to the Front on both floors, 2 double height rendered columns and horizontal connection on the Secondary Street side - Ekta.	



THIS DRAWING IS THE EXCLUSIVE PROPERTY OF THE DEVELOPER & THE REPRODUCTION OF ANY PART WITHOUT THE PRIOR WRITTEN CONSENT OF THE DEVELOPER IS A VIOLATION OF APPLICABLE LAWS. IN NO EVENT SHALL THE DEVELOPER BE HELD LIABLE FOR SPECIAL COLLATERAL, INCIDENTAL OR CONSEQUENTIAL LIABILITY IN CONNECTION WITH THE USE OF THIS DIGITAL DATA ONCE RELEASED FROM THE DEVELOPER'S OFFICE. THIS DRAWING IS TO BE READ & UNDERSTOOD IN CONJUNCTION WITH THE STRUCTURAL, MECHANICAL, ELECTRICAL & / OR ANY OTHER CONSULTANT'S DOCUMENTATION AS MAY BE APPLICABLE TO THE PROJECT PRIOR TO THE START OF ANY WORKS AND FOR ITS DURATION.

PROJECT:
2 GOUNDREY STREET


LOT 70 2 GOUNDREY STREET
CATHERINE FIELDS

DRAWING TITLE:
FLOOR AREA PLAN

NORTH:


LOT NO: 70	DATE: 15-09-2026	SCALE: 1 : 100	DRAWING No: CDC.11	REV: 7
DRAWN BY: AS	CHECKED BY: RH			
DRAFTED BY: SL	CLIENT NAME: Gopal Narayanappa & Shobha Srinivas Reddy			

CDC ISSUE

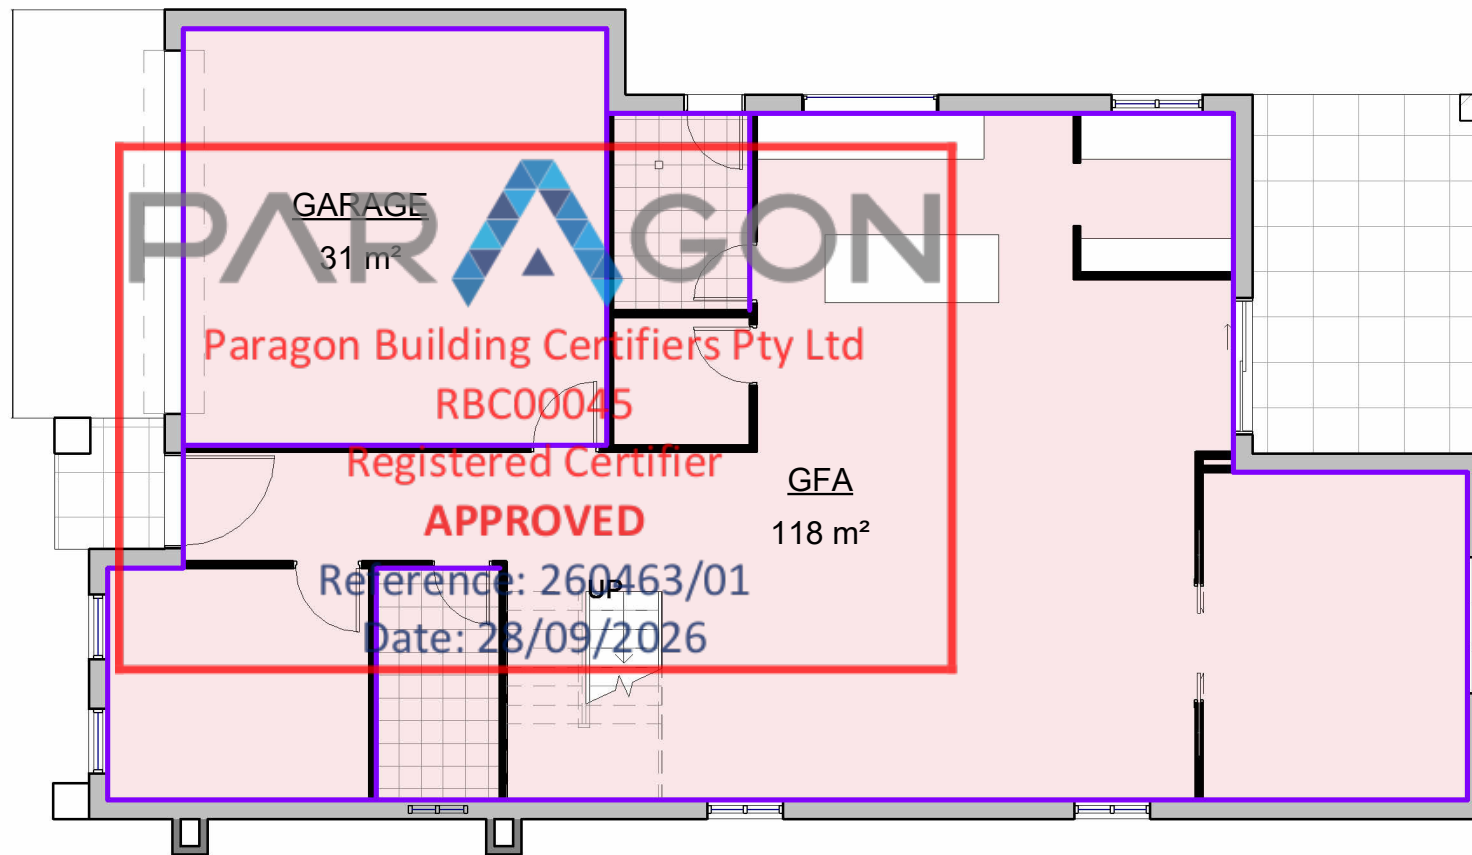

1 Ground Floor
1 : 100

Area Schedule (Rentable)	
Name	Area

Ground Floor

GFA	118 m ²
GARAGE	31 m ²


Ground Floor: 2 149 m²

Level 1

FFA	120 m ²
STAIR VOID	6 m ²

Level 1: 2 126 m²

Grand total: 4 275 m²

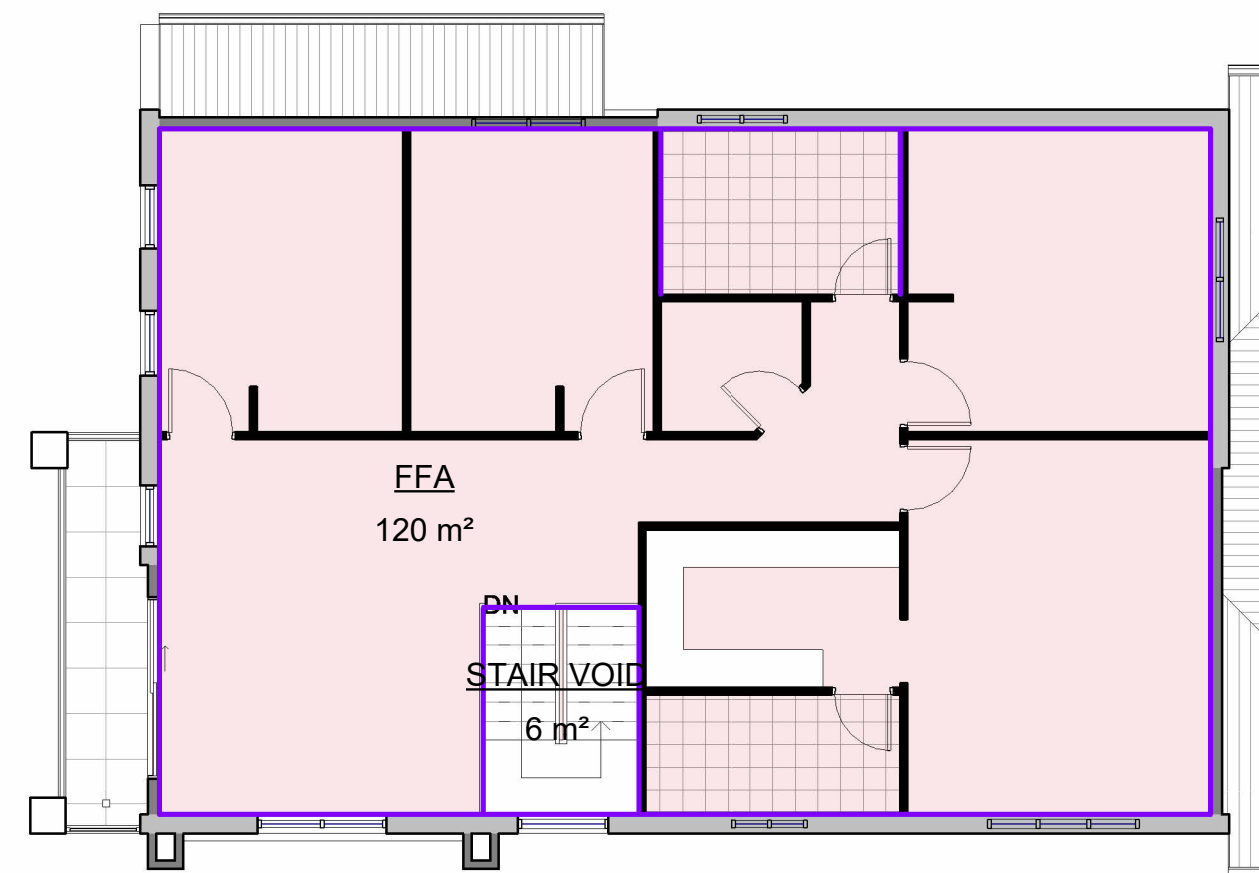

2 Level 1
1 : 100

REV	DATE	DESCRIPTION	BY
7	28-07-2026	CDC ISSUE	




THIS DRAWING IS THE EXCLUSIVE PROPERTY OF THE DEVELOPER & THE REPRODUCTION OF ANY PART WITHOUT THE PRIOR WRITTEN CONSENT OF THE DEVELOPER IS A VIOLATION OF APPLICABLE LAWS. IN NO EVENT SHALL THE DEVELOPER BE HELD LIABLE FOR SPECIAL COLLATERAL, INCIDENTAL OR CONSEQUENTIAL LIABILITY IN CONNECTION WITH THE USE OF THIS DIGITAL DATA ONCE RELEASED FROM THE DEVELOPER'S OFFICE. THIS DRAWING IS TO BE READ & UNDERSTOOD IN CONJUNCTION WITH THE STRUCTURAL, MECHANICAL, ELECTRICAL & / OR ANY OTHER CONSULTANT'S DOCUMENTATION AS MAY BE APPLICABLE TO THE PROJECT PRIOR TO THE START OF ANY WORKS AND FOR ITS DURATION.

PROJECT:
2 GOUNDREY STREET

LOT 70 2 GOUNDREY STREET
CATHERINE FIELDS

DRAWING TITLE:
**RENTABLE AREA
PLAN**

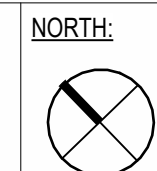

LOT NO: 70	DATE: 15-09-2026	SCALE: 1 : 100	DRAWING No: CDC.12	REV: 7
DRAWN BY: AS	CHECKED BY: RH			ISSUED BY:
DRAFTED BY: SL	CLIENT NAME: Gopal Narayanappa & Shobha Srinivas Reddy			



Paragon Building Certifiers Pty Ltd

RBC00045

Registered Certifier

APPROVED

Reference: 260463/01

Date: 28/09/2026



	1. RF	2. BR1	3. CD1	4. CR1	5. AL	6. ED	7. GD	8. FAS	9. GUT
	ROOF	MAIN WALLS	CLADDING	ACCENT 1/RENDER	WINDOWS/ BALUSTRADE	MAIN DOOR	GARAGE DOOR	FASCIA	GUTTER
MATERIAL	COLORBOND (DEEP OCEAN)	BRICK	BLUEBOARD	BRICK	ALUMINIUM	TIMBER	COLORBOND	COLORBOND	COLORBOND
COLOUR									

NOTE : ALL COLOURS SPECIFIED ARE INDICATIVE ONLY AND ARE SUBJECT TO VARIATION AND TO AVAILABILITY
ANY DISCREPANCY PLEASE FOLLOW AS PER RENDERED IMAGE

REV	DATE	DESCRIPTION	BY
7	28-07-2026	CDC ISSUE	



THIS DRAWING IS THE EXCLUSIVE PROPERTY OF THE DEVELOPER & THE REPRODUCTION OF ANY PART WITHOUT THE PRIOR WRITTEN CONSENT OF THE DEVELOPER IS A VIOLATION OF APPLICABLE LAWS. IN NO EVENT SHALL THE DEVELOPER BE HELD LIABLE FOR SPECIAL COLLATERAL, INCIDENTAL OR CONSEQUENTIAL LIABILITY IN CONNECTION WITH THE USE OF THIS DIGITAL DATA ONCE RELEASED FROM THE DEVELOPER'S OFFICE. THIS DRAWING IS TO BE READ & UNDERSTOOD IN CONJUNCTION WITH THE STRUCTURAL, MECHANICAL, ELECTRICAL & / OR ANY OTHER CONSULTANT'S DOCUMENTATION AS MAY BE APPLICABLE TO THE PROJECT PRIOR TO THE START OF ANY WORKS AND FOR ITS DURATION.

PROJECT:
2 GOUNDREY STREET


LOT 70 2 GOUNDREY STREET
CATHERINE FIELDS

DRAWING TITLE:
COLOR SCHEDULE

NORTH:

LOT NO:	DATE:	SCALE:	DRAWING No:	REV:
70	15-09-2026	1 : 100	CDC.14	7
DRAWN BY:	CHECKED BY:	ISSUED BY:		
AS	RH			
DRAFTED BY:	CLIENT NAME:			
SL	Gopal Narayanappa & Shobha Srinivas Reddy			

CDC ISSUE

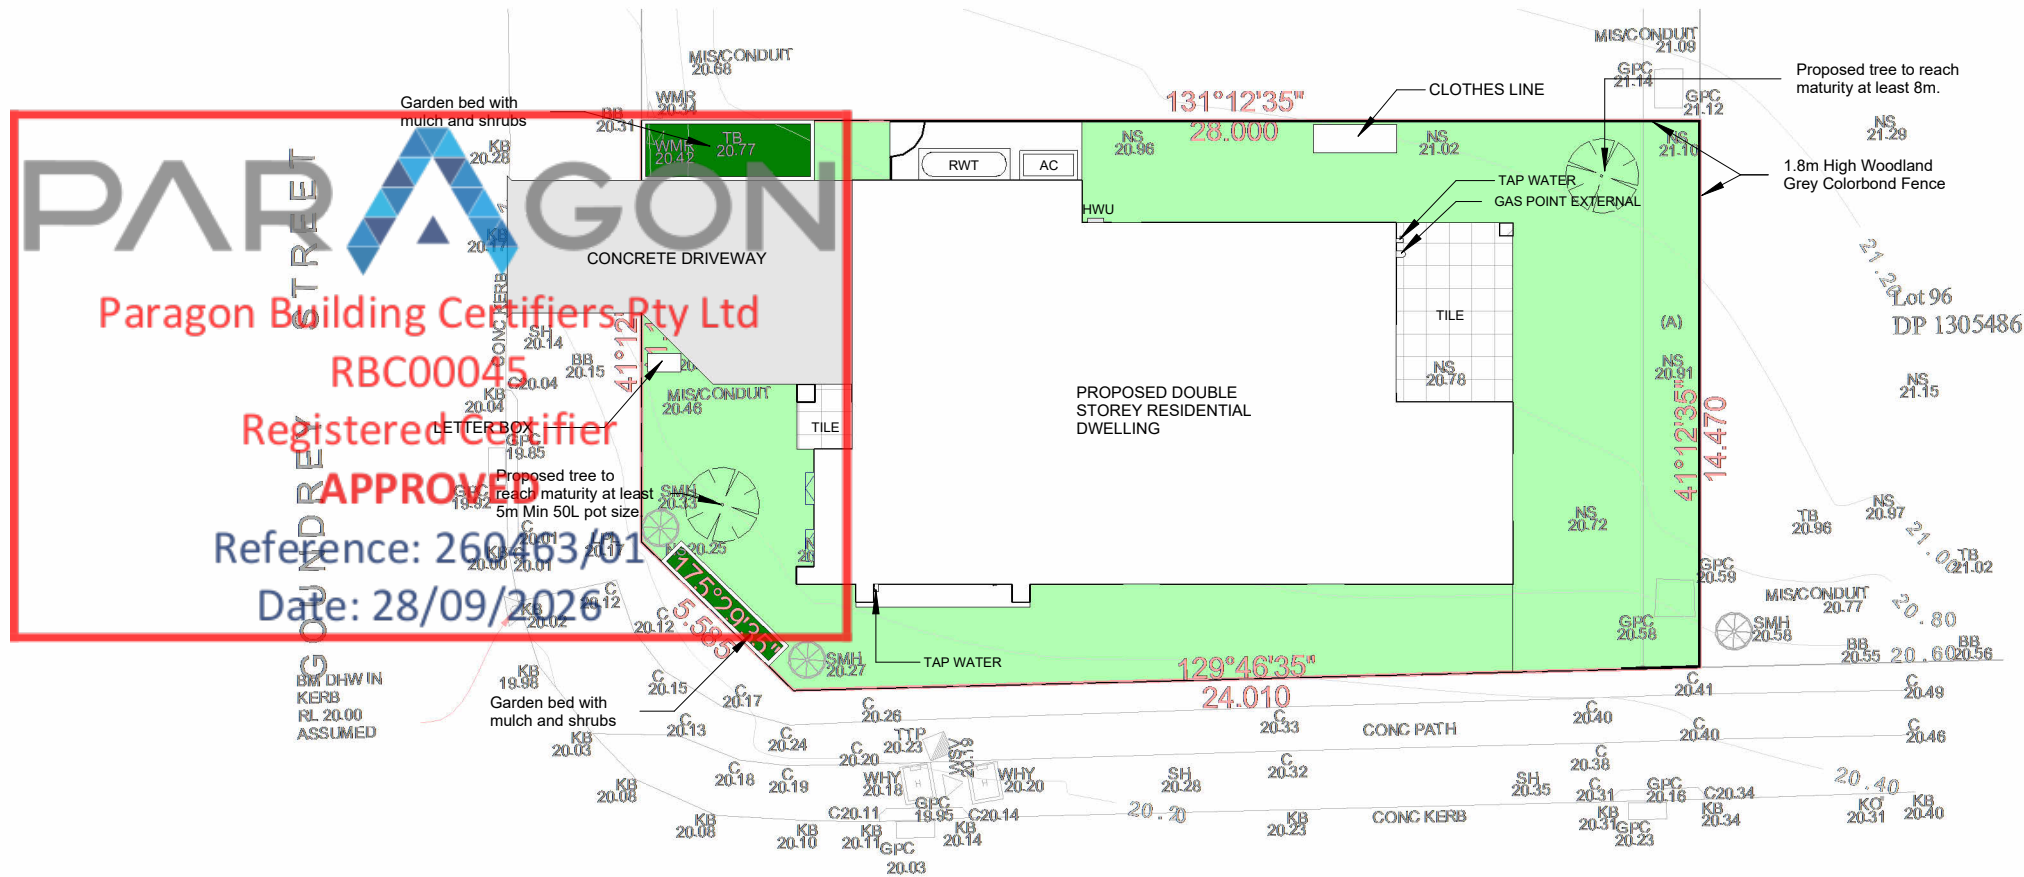

CDC - LANDSCAPE PLAN

1
1 : 200

McCLYMONT DRIVE

GENERAL NOTES:

- LANDSCAPE CONTRACTOR TO CHECK DA CONDITIONS AND STAMPED LANDSCAPE PLAN
- BEFORE COMMENCING WORKS TO ENSURE NO ADDITIONS/AMENDMENTS TO PLAN.
- GARDEN BEDS IN OSD BASIN TO CONSIST OF NON FLOATABLE DECORATIVE GRAVEL.
- REFER TO HYDRAULICS ENGINEERS PLAN FOR OSD DETAILS/FINAL LEVELS.
- MULCHED PLANTING BEDS TO BE A MINIMUM DEPTH OF 75mm AS SELECTED.
- CONTRACTOR'S RESPONSIBILITY TO CHECK AND ADJUST SOIL pH AS REQUIRED.
- PROVIDE TIMBER EDGE AS A MINIMUM BENEATH FENCING/GATES TO DEFINE TURF AND GARDEN BEDS/PATHWAYS, EDGING TO BE PROVIDED TO ALL AREAS WHERE DIFFERING MATERIALS MEET i.e TURF/GARDEN, TURF/GRAVEL PATH ETC.
- WEED MAT BENEATH GRAVEL GRAVEL PATHWAYS REQUIRED TO LIMIT MUD TRACKING.
- PREMIUM ORGANIC GARDEN MIX TO BE USED.
- ALL PLANTS TO BE HEALTHY AND VIGOROUS.
- CONTRACTOR TO MAKE GOOD TURF ON NATURE STRIP POST CONSTRUCTION.
- CONTRACTOR TO MAKE GOOD TURF ON NATURE STRIP POST CONSTRUCTION.
- DO NOT SCALE ARCHITECTURAL SETOUT FROM LANDSCAPE DRAWING.
- EXISTING TREE SPREAD APPROXIMATE ONLY. REFER TO TREE REPORT WHEN APPLICABLE.
- SITE SURVEY PROVIDED BY OTHERS.
- BUFFALO TURF PREFERRED OVER KIKUYU.

LANDSCAPE BASIX NOTE:

THE APPLICANT MUST PLANT INDIGENEOUS OR LOW WATER USE SPECIES OF VEGETATION THROUGHOUT 15 SQM OF THE SITE.

NOTE : BUILDER RESERVES THE RIGHT NOT TO UNDERTAKE NOR SUPPLY CERTIFICATE FOR OCCUPATION CERTIFICATE.


NOTE : TO AID COMPLIANCE WITH BASIX LEGISLATION, PLANTS (WHERE APPLICABLE) HAVE BEEN SELECTED FROM THE LOCAL CITY COUNCIL/SHIRE PLANT LISTS.

NOTE: LOCATION OF SEWER MAINS/LINES, WATER PIPES, UNDERGROUND ELECTRICITY AND OTHER SERVICES MUST BE OBTAINED PRIOR TO COMMENCEMENT OF ANY WORK ON SITE.

CONTRACTORS NOTE : CALCULATED AREAS DETERMINED BY CAD AND HAVE BEEN ROUNDED UP FOR USE AS A GUIDE ONLY ALLOW STANDARD PERCENTAGE FOR CUTTING AND WASTAGE .CONFIRM DIMENSIONS AND NUMBERS PRIOR TO QUOTING/ORDERING.


LANDSCAPE AREA

FRONT AREA	87.4 m ²
BACKYARD AREA	102.9 m ²
TOTAL AREA	190.3 m ²

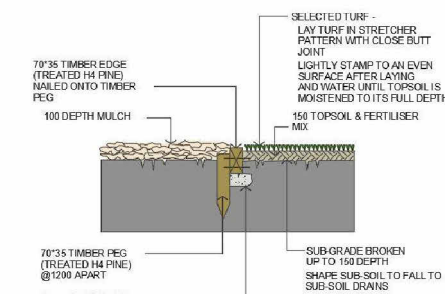

1. TURF & GARDEN EDGE DETAIL

NOTE:
ALIGNMENT OF BRICK EDGE SHALL BE EVEN & FREE FROM
DIPS AND HUMPS

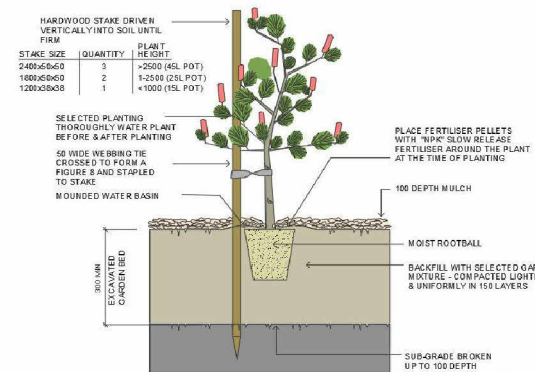

2. TREE & SHRUB PLANTING IN GARDEN BED

NOTE:
DO NOT PLANT IN UNSUITABLE WEATHER CONDITIONS
SUCH AS EXTREME HEAT, COLD, WIND OR RAIN
CLAY SOIL IS TO BE TREATED WITH CLAY BREAKER
AND ORGANIC COMPOST

CDC ISSUE

REV	DATE	DESCRIPTION	BY
9	15-09-2026	470x470 feature column added, FW6 shifted towards Secondary facade - Krishna	
7	28-07-2026	CDC ISSUE	




THIS DRAWING IS THE EXCLUSIVE PROPERTY OF THE DEVELOPER & THE REPRODUCTION OF ANY PART WITHOUT THE PRIOR WRITTEN CONSENT OF THE DEVELOPER IS A VIOLATION OF APPLICABLE LAWS. IN NO EVENT SHALL THE DEVELOPER BE HELD LIABLE FOR SPECIAL COLLATERAL, INCIDENTAL OR CONSEQUENTIAL LIABILITY IN CONNECTION WITH THE USE OF THIS DIGITAL DATA ONCE RELEASED FROM THE DEVELOPER'S OFFICE. THIS DRAWING IS TO BE READ & UNDERSTOOD IN CONJUNCTION WITH THE STRUCTURAL, MECHANICAL, ELECTRICAL & / OR ANY OTHER CONSULTANT'S DOCUMENTATION AS MAY BE APPLICABLE TO THE PROJECT PRIOR TO THE START OF ANY WORKS AND FOR ITS DURATION.

PROJECT:
2 GOUNDREY STREET

LOT 70 2 GOUNDREY STREET
CATHERINE FIELDS

DRAWING TITLE:
LANDSCAPE PLAN

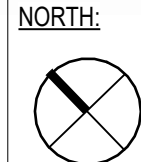

LOT NO: 70	DATE: 15-09-2026	SCALE: 1 : 200	DRAWING No: CDC.15	REV: 9
DRAWN BY: AS	CHECKED BY: RH			ISSUED BY:
DRAFTED BY: SL	CLIENT NAME: Gopal Narayanappa & Shobha Srinivas Reddy			

ABCB HOUSING PROVISIONS : PART 10.2 WET AREA WATERPROOFING

10.2.1 Wet Areas

- 1. Building elements in wet areas within a building must be protected with a waterproofing system.
- 2. The waterproofing system in (1) must be either waterproof or water resistant in accordance with 10.2.2 to 10.2.6.

10.2.2 Shower Area (enclosed and unenclosed)

- 1. For a shower area with a hob, step-down or level threshold, the following applies:
 - a. The floor of the shower area must be waterproof, including any hob or step-down (see Figure 10.2.2); and
 - b. The walls of the shower area must be waterproof not less than 1800 mm above the floor substrate (see Figure 10.2.2).
 - c. Wall junctions and joints within the shower area must be waterproof not less than 40 mm either side of the junction (see Figure 10.2.2).
 - d. Wall/floor junctions within the shower area must be waterproof (see Figure 10.2.2).
 - e. Penetrations within the shower area must be waterproof.
- 2. A shower with a preformed shower base must also comply with the requirements of (1), except for (a) which is not applicable.

Figure 10.2.2: Extent of treatment for shower areas - concrete compressed fibre-cement and fibre-cement sheet floors.

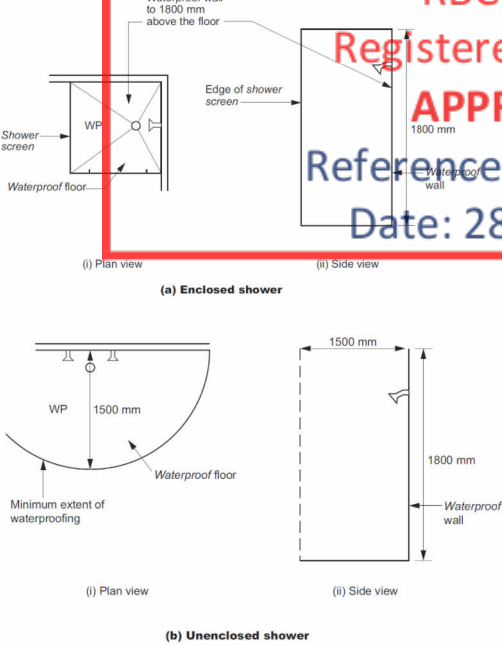


Figure Notes
Wall/floor junction heights are to be as per 10.2.2 to 10.2.6 (as applicable).

Notes
Where a shower is above a bath or spa, use requirements for shower.

10.2.3 Area outside shower area

- 1. For concrete, compressed fibre-cement and fibre-cement sheet flooring, the floor of the room must be water resistant.
- 2. For timber floors including particleboard, plywood and other timber based flooring materials, the floor of the room must be waterproof.
- 3. Wall/floor junctions must be -
 - a. waterproof, and
 - b. where a flashing is used, the horizontal leg must be not less than 40 mm.

10.2.4 Areas adjacent to baths and spas without showers

- 1. For areas adjacent to all baths and spas, the following applies:
 - a. For concrete, compressed fibre-cement and fibre-cement sheet flooring, the floor of the room must be water resistant.
 - b. For timber floors including particleboard, plywood and other timber based flooring materials, the floor of the room must be waterproof.
 - c. Tap and spout penetrations must be waterproof where they occur in horizontal surfaces.
- 2. For areas adjacent to non-freestanding baths and spas, the following applies:
 - a. Walls must be water resistant (see Figure 10.2.4a and Figure 10.2.4b)-
 - to a height of not less than 150mm above the vessel, for the extent of the vessel, where the vessel is within 75mm of a wall, and
 - for all exposed surfaces below vessel lip.
 - b. Wall junctions and joints must be water resistant within 150mm above a vessel for the extent of the vessel.
 - c. Wall/floor junctions must be waterproof for the extent of the vessel (see Figure 10.2.4a and Figure 10.2.4b).
- 3. For inserted baths and spas, the following applies:
 - a. For floors and horizontal surfaces:
 - Any shelf area adjoining the bath or spa must be waterproof and include a waterstop under the vessel lip.
 - There are no requirements for the floor under a bath or spa.
 - b. For walls:
 - Waterproof to not less than 150mm above the lip of a bath or spa.
 - There are no requirements for the floor under a bath or spa.
 - c. For wall junctions and joints, the following applies:
 - Waterproof junctions within 150mm of a bath or spa.
 - There are no requirements for junctions and joints in walls beneath the lip of a bath or spa.
 - d. Tap and spout penetrations must be waterproof where they occur in horizontal surfaces.

Figure 10.2.4a: Areas adjacent to baths and spas without showers for concrete, compressed fibre-cement and fibre-cement sheet flooring


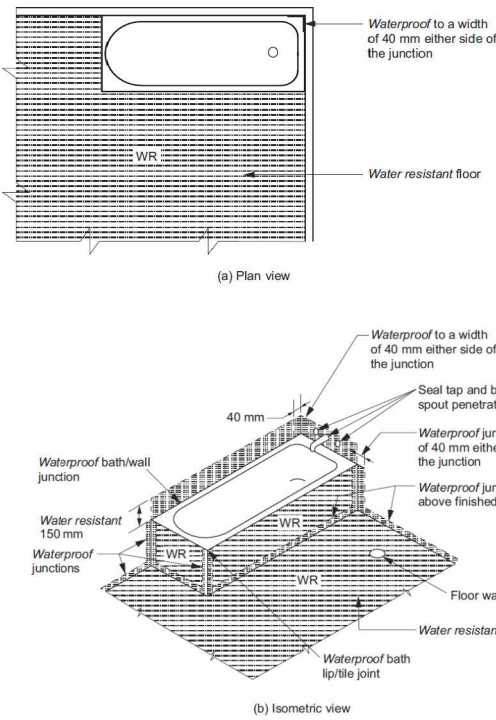



Figure 10.2.4b: Areas adjacent to baths and spas without showers for timber floors including particle-board, plywood and other floor materials

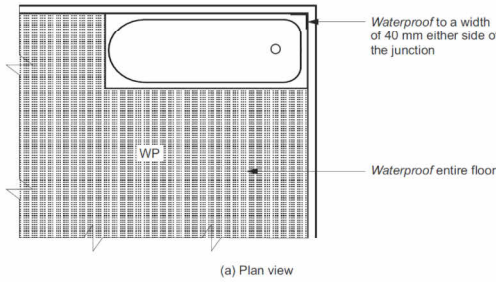

10.2.5 Other areas

- 1. For walls adjoining other types of vessels (e.g. sink, basin or laundry tub), the following applies:
 - a. Walls must be water resistant to a height of not less than 150mm above the vessel, for the extent of the vessel, where the vessel is within 75 mm of a wall (see Figure 10.2.5.)
 - b. Waterproof wall junctions where a vessel is fixed to a wall.
 - c. Waterproof tap and spout penetrations where they occur in surfaces required to be waterproof or water resistant.
- 2. For laundries and WCs, the following applies:
 - a. The floor of the room must be water resistant.
 - b. Wall/floor junctions must be water resistant, and where a flashing is used, the horizontal leg must not be less than 40 mm.
- 3. For WCs with handheld bidet spray installations, the following applies:
 - a. The floor of the room must be waterproof.
 - b. Walls must be -
 - waterproof in WC area within a 900 mm radius from the wall connection of the handheld bidet spray device to a height of not less than 150mm above the floor substrate; and
 - water resistant in WC area within a 900 mm radius from the wall connection of the handheld bidet device to not less than 1200 mm above the finished floor level of the WC.
 - c. Wall junctions within the WC area within 900 mm radius from the wall connection of the handheld bidet spray device must be waterproof.
 - d. Wall/floor junctions within the WC area within 1000 mm radius from the wall connection of the handheld bidet spray device must be waterproof.
 - e. Penetrations in the WC area must be waterproof.

Figure 10.2.5: Bath and vessel abutting wall - areas to be protected

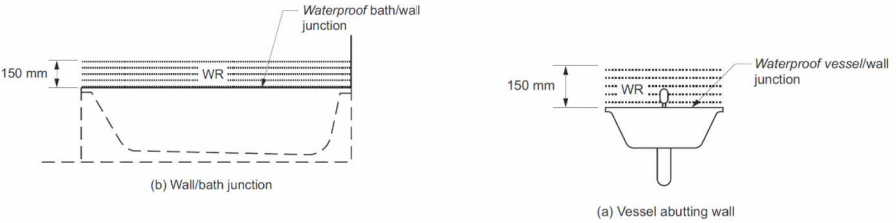

10.2.6 Waterproofing systems

- 1. For the purposes of this Part, a waterproofing system is deemed -
 - a. waterproof, if it complies with (2); or
 - b. water resistant, if it complies with (3).
- 2. For a waterproofing system required to be waterproof in accordance with 10.2.2 to 10.2.5, the materials nominated in 10.2.8 must be used.
- 3. For a waterproofing system required to be water resistant in accordance with 10.2.2 to 10.2.5, the materials nominated in 10.2.9 must be used in conjunction with the materials in 10.2.10.

10.2.12 Construction of wet area floors - falls

Where a floor waste is installed -

- a. the minimum continuous fall of a floor plane to the waste must be 1:80; and
- b. the maximum continuous fall of a floor plane to the waste must be 1:50.

				CDC ISSUE								
				 THIS DRAWING IS THE EXCLUSIVE PROPERTY OF THE DEVELOPER & THE REPRODUCTION OF ANY PART WITHOUT THE PRIOR WRITTEN CONSENT OF THE DEVELOPER IS A VIOLATION OF APPLICABLE LAWS. IN NO EVENT SHALL THE DEVELOPER BE HELD LIABLE FOR SPECIAL COLLATERAL, INCIDENTAL OR CONSEQUENTIAL LIABILITY IN CONNECTION WITH THE USE OF THIS DIGITAL DATA ONCE RELEASED FROM THE DEVELOPER'S OFFICE. THIS DRAWING IS TO BE READ & UNDERSTOOD IN CONJUNCTION WITH THE STRUCTURAL, MECHANICAL, ELECTRICAL & / OR ANY OTHER CONSULTANT'S DOCUMENTATION AS MAY BE APPLICABLE TO THE PROJECT PRIOR TO THE START OF ANY WORKS AND FOR ITS DURATION.	PROJECT: 2 GOUNDREY STREET LOT 70 2 GOUNDREY STREET CATHERINE FIELDS	DRAWING TITLE: WATERPROOFING DETAILS	NORTH:	LOT NO:	DATE:	SCALE: 1 : 50	DRAWING No:	REV:
7	28-07-2026	CDC ISSUE						70	15-09-2026			7
REV	DATE	DESCRIPTION	BY					DRAWN BY:	CHECKED BY:			ISSUED BY:
								AS	RH			
								DRAFTED BY:	CLIENT NAME:			
								SL	Gopal Narayanappa & Shobha Srinivas Reddy			