

FOR CONSTRUCTION

LOT 2322 1 HOPPLES ROAD MENANGLE PARK

PROPOSED CONSTRUCTION OF A SINGLE STOREY DWELLING



BASIX COMMITMENTS	Certificate number: 1866043S_02
	Date of issue: Tuesday, 29 September 2026
WATER	
LANDSCAPE	237m2
TOILETS	5 STARS
KITCHEN TAPS	5 STARS
SHOWER HEADS	5 STARS (>4.5 but <=6 Umin)
BASIN TAPS	5 STARS
ALTERNATIVE WATER	1500L RAINWATER TANK
ROOF WATER TO TANK	346 m2
ALT.WATER USES- TANK	LAUNDRY
ALT. WATER USES - RETIC	ALL TOILETS + ONE OUTDOOR TAP
SWIMMING POOL	N/A
ENERGY	
HOT WATER	GAS INSTANTANEOUS - 5 STAR
AIR-CON (HEATING)	3 PHASE DUCTED - EER 3.0-3.5
AIR-CON (COOLING)	3 PHASE DUCTED - EER 3.0-3.5
VENTILATION - BATHROOM	NONE/ NATURAL VENTILATION
VENTILATION - KITCHEN	DUCTED - MANUAL SWITCH
VENTILATION - LAUNDRY	DUCTED - INTERLOCKED TO LIGHT
PV SYSTEM	N/A
COOKTOP	GAS
OVEN	ELECTRIC
CLOTHES DRYING	OUTDOOR CLOTHESLINE
LIGHTING	DEDICATED LED

GENERAL LEGEND	
AC	AIR CONDITIONING UNIT
AL	POWDERCOATED ALUMINIUM DOOR/ WINDOW
BAL	BALUSTRADE TYPE
BG	BOX GUTTER
BR1, BR2, etc.	BRICK FACE TYPE
CAP	METAL CAPPING
CD1, CD2, etc.	WALL CLADDING
CONC.	CONCRETE FLOOR
CPT	CARPET
CRT	CONCRETE ROOF TILES
CR1, CR2, etc.	CEMENT RENDER TYPE/ COLOUR
DP/S	DOWN PIPE
DW	DISH WASHER
ED	ENTRY DOOR
F	FRIDGE
FAS	FASCIA
FET	FEATURE TILE
FT, FT1, FT2, etc	FLOOR TILES
FW	FLOOR WASTE
GD	GARAGE DOOR
GUT	GUTTER
HWU	HOT WATER UNIT
HYB	HYBRID FLOOR
L	LINEN
MR	METAL ROOF
MW	MICROWAVE OVEN
NGL	NATURAL GROUND LEVEL
OBS	OBSCURED GLASS
P	PANTRY
R	ROBE
RL	REDUCED LEVEL
RWH	RAIN WATER HEAD
RWT	RAIN WATER TANK
S	STORAGE
TOW	TOP OF WALL
TL	TIMBER LAMINATE
WC	WATER CLOSET
WM	WASHING MACHINE
SD	SMOKE DETECTOR

Sheet List		
Sheet No.	Sheet Name	Revision
CDC.01	COVER SHEET	2
CDC.02A	GENERAL NOTES	2
CDC.02B	GENERAL NOTES	2
CDC.03	LOCATION PLAN AND SITE PLAN	2
CDC.04	SITE ANALYSIS AND SEDIMENT CONTROL	2
CDC.05	GROUND FLOOR PLAN	2
CDC.07	ROOF PLAN	2
CDC.08	ELEVATION 01	2

Sheet List		
Sheet No.	Sheet Name	Revision
CDC.09	ELEVATION 02	2
CDC.10	SECTIONS	2
CDC.11	FLOOR AREA PLAN	2
CDC.12	RENTABLE AREA PLAN	2
CDC.14	COLOR SCHEDULE	2
CDC.15	LANDSCAPE PLAN	2
CDC.16	WATERPROOFING DETAILS	2

NOTE.: ALL IMAGES ARE FOR ILLUSTRATION ONLY AND ARE SUBJECT TO VARIATION AS PER SITE CONDITION, STRUCTURAL ELEMENT AND TO AVAILABILITY OF MATERIALS.

2	7-08-2026	CDC ISSUE	
REV	DATE	DESCRIPTION	BY



THIS DRAWING IS THE EXCLUSIVE PROPERTY OF THE DEVELOPER & THE REPRODUCTION OF ANY PART WITHOUT THE PRIOR WRITTEN CONSENT OF THE DEVELOPER IS A VIOLATION OF APPLICABLE LAWS. IN NO EVENT SHALL THE DEVELOPER BE HELD LIABLE FOR SPECIAL COLLATERAL, INCIDENTAL OR CONSEQUENTIAL LIABILITY IN CONNECTION WITH THE USE OF THIS DIGITAL DATA ONCE RELEASED FROM THE DEVELOPER'S OFFICE. THIS DRAWING IS TO BE READ & UNDERSTOOD IN CONJUNCTION WITH THE STRUCTURAL, MECHANICAL, ELECTRICAL & / OR ANY OTHER CONSULTANT'S DOCUMENTATION AS MAY BE APPLICABLE TO THE PROJECT PRIOR TO THE START OF ANY WORKS AND FOR ITS DURATION.

PROJECT:
LOT 2322 1 HOPPLES ROAD
1 HOPPLES ROAD MENANGLE PARK

DRAWING TITLE:
COVER SHEET

NORTH:

LOT NO: 2322	DATE: 24-09-2026	SCALE: As indicated	<u>DRAWING</u> No: CDC.01	<u>REV:</u> 2
DRAWN BY: AS	CHECKED BY: RH	ISSUED BY:		
DRAFTED BY: SL	CLIENT NAME: Owner			

BUILDING SPECIFICATIONS

National Construction Code – Volume 2,
Amendment 1 – Building Code of Australia 2022
& Housing Provisions Standard 2022

SITE PREPARATION

- PART 3.1 OF THE NCC VOLUME 2, AMENDMENT 1 - BUILDING CODE OF AUSTRALIA 2022 & HOUSING PROVISIONS STANDARD 2022.

EARTHWORKS

- TO BE CARRIED OUT IN ACCORDANCE WITH THE REQUIREMENTS OF THE ENVIRONMENTAL PLANNING & ASSESSMENT ACT 1979 AND DEVELOPMENT CONSENT CONDITIONS
- PART 3.2 OF THE NCC VOLUME 2, AMENDMENT 1 - BUILDING CODE OF AUSTRALIA 2022 & HOUSING PROVISIONS STANDARD 2022.
- AS 4678:2002 - EARTH-RETAINING STRUCTURES

DRAINAGE

- PART 3.3 OF THE NCC VOLUME 2, AMENDMENT 1 - BUILDING CODE OF AUSTRALIA 2022 & HOUSING PROVISIONS STANDARD 2022.
- AS/NZS 3500.1:2021 - PLUMBING & DRAINAGE - WATER SERVICES
- AS/NZS 3500.2:2021 - PLUMBING & DRAINAGE - SANITARY PLUMBING & DRAINAGE
- AS/NZS 3500.3:2021 - PLUMBING & DRAINAGE STORMWATER DRAINAGE
- AS/NZS 3500.4:2021 - PLUMBING & DRAINAGE - HEATED WATER SERVICES

STRUCTURAL WORK

- Part 2.2 OF THE NCC VOLUME 2, AMENDMENT 1 - BUILDING CODE OF AUSTRALIA 2022 & HOUSING PROVISIONS STANDARD 2022.
- AS 4100:2020- STEEL STRUCTURES CODES
- AS/NZS 1170.0:2002 – GENERAL PRINCIPLES
- AS/NZS 1170.1:2002 – PARTS 1 PERMANENT, IMPOSED AND OTHER ACTIONS
- AS/NZS 1170.2:2021 – PART 2 WIND ACTIONS
- AS 3700:2018- SAA MASONRY CODE
- AS 1684.3:2021- RESIDENTIAL TIMBER FRAMED CONSTRUCTION

FOOTINGS & SLABS

- PART 4 OF THE NCC VOLUME 2, AMENDMENT 1 - BUILDING CODE OF AUSTRALIA 2022 & HOUSING PROVISIONS STANDARD 2022.
- AS 2159:2009 - PILING - DESIGN & INSTALLATION
- AS 2870:2011 - RESIDENTIAL SLABS & FOOTINGS
- AS 3600:2018 - CONCRETE STRUCTURES

MASONRY

- PART 5 OF THE NCC VOLUME 2, AMENDMENT 1 - BUILDING CODE OF AUSTRALIA 2022 & HOUSING PROVISIONS STANDARD 2022.
- AS 3700:2018 - MASONRY STRUCTURES

FRAMING

- PART 6 OF THE NCC VOLUME 2, AMENDMENT 1 - BUILDING CODE OF AUSTRALIA 2022 & HOUSING PROVISIONS STANDARD 2022.
- AS 1684.2:2021 - RESIDENTIAL TIMBER-FRAMED CONSTRUCTION - NON- CYCLONIC AREAS
- AS 1720.1:2010 - TIMBER STRUCTURES - DESIGN METHODS
- AS 4100:2020 - STEEL STRUCTURES
- AS 3660.1:2014 – TERMITE MANAGEMENT SYSTEM

ROOF & WALL CLADDING

- PART 7 OF THE NCC VOLUME 2, AMENDMENT 1 - BUILDING CODE OF AUSTRALIA 2022 & HOUSING PROVISIONS STANDARD 2022.
- AS 1273:1991 - UNPLASTICIZED PVC (UPVC) DOWNPIPES & FITTINGS FOR RAINWATER
- AS 1562.1:2018 - DESIGN & INSTALLATION OF SHEET ROOF & WALL CLADDING - METAL
- AS/NZS 1562.3:2006 - DESIGN & INSTALLATION OF SHEET ROOF & WALL CLADDING - PLASTIC
- AS 2049:2002 - ROOF TILES
- AS 2050:2018 - INSTALLATION OF ROOF TILES
- AS 4285:2019 – ROOFLIGHTS

GLAZING

- PART 8 OF THE NCC VOLUME 2, AMENDMENT 1 - BUILDING CODE OF AUSTRALIA 2022 & HOUSING PROVISIONS STANDARD 2022.
- AS 1288:2021 - GLASS IN BUILDINGS - SELECTION & INSTALLATION
- AS 2047:2014 - WINDOWS & EXTERNAL GLAZED DOORS IN BUILDINGS
- AS/NZS 2208:1996 - SAFETY GLAZING MATERIALS IN BUILDINGS

FIRE SAFETY

- PART 9 OF THE NCC VOLUME 2, AMENDMENT 1 - BUILDING CODE OF AUSTRALIA 2022 & HOUSING PROVISIONS STANDARD 2022.
- AS 3786:2014 - SMOKE ALARMS USING SCATTERED LIGHT, TRANSMITTED LIGHT OR IONIZATION

HEALTH & AMENITY

- PART 10 OF THE NCC VOLUME 2, AMENDMENT 1 - BUILDING CODE OF AUSTRALIA 2022 & HOUSING PROVISIONS STANDARD 2022.
- AS/NZS ISO 717.1:2004 - ACOUSTICS - RATING OF SOUND INSULATION IN BUILDINGS & OF BUILDING ELEMENTS - AIRBORNE SOUND INSULATION
- AS ISO 717.2:2004 - ACOUSTICS - RATING OF SOUND INSULATION IN BUILDINGS & OF BUILDING ELEMENTS - IMPACT SOUND INSULATION
- AS 1668.2:2012 - THE USE OF VENTILATION & AIR CONDITIONING IN BUILDINGS - MECHANICAL VENTILATION IN BUILDINGS
- AS 1668.4:2012 - THE USE OF VENTILATION & AIR CONDITIONING IN BUILDINGS - NATURAL VENTILATION OF BUILDINGS
- AS/NZS 1680.0:2009 - INTERIOR LIGHTING - SAFE MOVEMENT
- AS 3740:2021 - WATERPROOFING OF DOMESTIC WET AREAS
- AS 3000:2018 – ELECTRICAL INSTALLATION
- BCA Part 10.8.1, AS4200.1 & AS4200.2 – PLIABLE BUILDING MEMBRANE INSTALLED.

WATERPROOFING

- PART 10.2 OF THE NCC VOLUME 2, AMENDMENT 1 - BUILDING CODE OF AUSTRALIA 2022 & HOUSING PROVISIONS STANDARD 2022
- AS 3740:2021 – WATERPROOFING TO WET AREA
- AS 4654:2012 – EXTERNAL WET AREAS

SAFE MOVEMENT & ACCESS

- PART 11 OF THE NCC VOLUME 2, AMENDMENT 1 - BUILDING CODE OF AUSTRALIA 2022 & HOUSING PROVISIONS STANDARD 2022.
- AS 1428.1:2009 - DESIGN FOR ACCESS & MOBILITY – GENERAL REQUIREMENTS FOR ACCESS - NEW BUILDING WORK
- AS 1657:2018 - FIXED PLATFORMS, WALKWAYS, STAIRWAYS & LADDERS - DESIGN, CONSTRUCTION & INSTALLATION

HANDRAILS & BALUSTRADE

- PART 11.3.3 OF THE NCC VOLUME 2, AMENDMENT 1 - BUILDING CODE OF AUSTRALIA 2022 & HOUSING PROVISIONS STANDARD 2022.
- PART 11.3.4 OF THE NCC VOLUME 2, AMENDMENT 1 - BUILDING CODE OF AUSTRALIA 2022 & HOUSING PROVISIONS STANDARD 2022.
- PART 11.3.5 OF THE NCC VOLUME 2, AMENDMENT 1 - BUILDING CODE OF AUSTRALIA 2022 & HOUSING PROVISIONS STANDARD 2022.
- AS 1170.1:2002 – BALUSTRADE INSTALLATION

PROTECTION OF OPENABLE WINDOW

PART 11.3.7 AND 11.3.8 OF THE NCC VOLUME 2, AMENDMENT 1 - BUILDING CODE OF AUSTRALIA 2022 & HOUSING PROVISIONS STANDARD 2022.

ENERGY EFFICIENCY

- PART 13 OF THE NCC VOLUME 2, AMENDMENT 1 - BUILDING CODE OF AUSTRALIA 2022 & HOUSING PROVISIONS STANDARD 2022 & BASIX CERTIFICATE.

MECHANICAL VENTILATION

- EXHAUST FROM A BATHROOM, SANITARY COMPARTMENT TO DISCHARGE DIRECTLY TO OUTDOOR AIR WITH MINIMUM FLOW RATE OF 25L/S & MAKE-UP AIR VIA OPENINGS TO AN ADJACENT ROOM WITH A FREE AREA OF 14,000 MM². THIS EXHAUST SYSTEM MUST BE INTERLOCKED WITH LIGHT SWITCH AND INCLUDE RUN-ON TIMER SO THAT THE EXHAUST SYSTEM CONTINUES TO OPERATE FOR 10 MINUTES AFTER THE LIGHT SWITCH IS OFF.
- ANY INSTALLED - KITCHEN RANGEHOOD EXHAUST TO DISCHARGE DIRECTLY OR VIA DUCT TO OUTDOOR AIR WITH MINIMUM FLOW RATE OF 40L/S & MAKE-UP AIR VIA OPENINGS TO AN ADJACENT ROOM WITH A FREE AREA OF 14,000 MM².
- LAUNDRY EXHAUST TO DISCHARGE DIRECTLY OR VIA DUCT TO OUTDOOR AIR WITH MINIMUM FLOW RATE OF 40L/S & MAKE-UP AIR VIA OPENINGS TO AN ADJACENT ROOM WITH A FREE AREA OF 14,000 MM².



2	7-08-2026	CDC ISSUE	
REV	DATE	DESCRIPTION	BY



THIS DRAWING IS THE EXCLUSIVE PROPERTY OF THE DEVELOPER & THE REPRODUCTION OF ANY PART WITHOUT THE PRIOR WRITTEN CONSENT OF THE DEVELOPER IS A VIOLATION OF APPLICABLE LAWS. IN NO EVENT SHALL THE DEVELOPER BE HELD LIABLE FOR SPECIAL COLLATERAL, INCIDENTAL OR CONSEQUENTIAL LIABILITY IN CONNECTION WITH THE USE OF THIS DIGITAL DATA ONCE RELEASED FROM THE DEVELOPER'S OFFICE. THIS DRAWING IS TO BE READ & UNDERSTOOD IN CONJUNCTION WITH THE STRUCTURAL, MECHANICAL, ELECTRICAL & / OR ANY OTHER CONSULTANT'S DOCUMENTATION AS MAY BE APPLICABLE TO THE PROJECT PRIOR TO THE START OF ANY WORKS AND FOR ITS DURATION.

PROJECT:
LOT 2322 1 HOPPLES ROAD
1 HOPPLES ROAD MENANGLE PARK

DRAWING TITLE:
GENERAL NOTES


NORTH:					
LOT NO:	2322	DATE:	24-09-2026	SCALE:	1 : 2
DRAWN BY:	AS	CHECKED BY:	RH	CDC.02A	
DRAFTED BY:	SL	CLIENT NAME:	Owner		

CDC ISSUE

DRAWING No:	2
ISSUED BY:	

TERMITE SHEET

- TERMITE SHEET EXTENDS THROUGH THE ENTIRE MASONRY LEAF AND IS VISIBLE AT THE FINISHED FACE OF THE WALL.

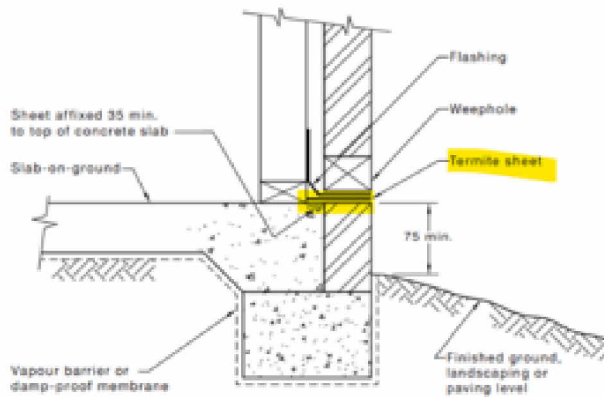


(a) Masonry veneer with separate strip footings

DIMENSIONS IN MILLIMETRES

FIGURE 5.5 (in part) TYPICAL SHEET INSTALLATION TO EXTERNAL WALL WITH CONCRETE FLOOR SLAB

DPC FOR BRICKS

DAMP-PROOF COURSE (DPC) TO EXTENDS THROUGH THE ENTIRE MASONRY LEAF AND NEED TO BE VISIBLE AT THE FINISHED FACE OF THE WALL FROM OUTSIDE

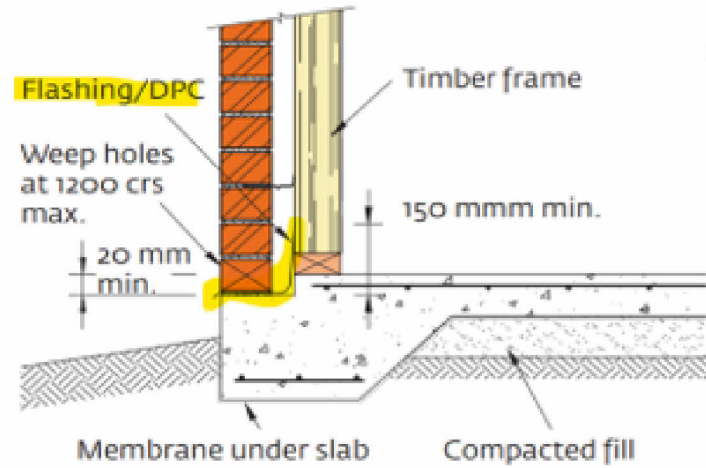

DEMOLITION

- AS 2601-2001 – DEMOLITION WORK

PLANTER BOX

REFER BELOW DETAILS FOR PLANTER BOX.


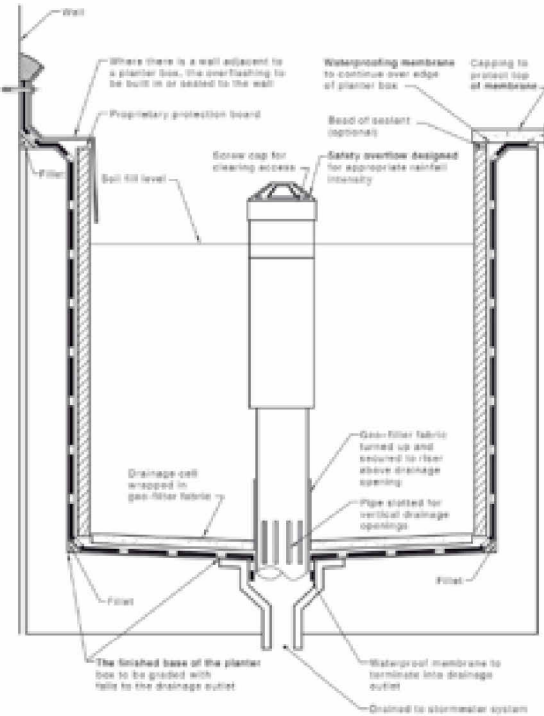



FIGURE 2.17 TYPICAL PLANTER BOX CONSTRUCTION

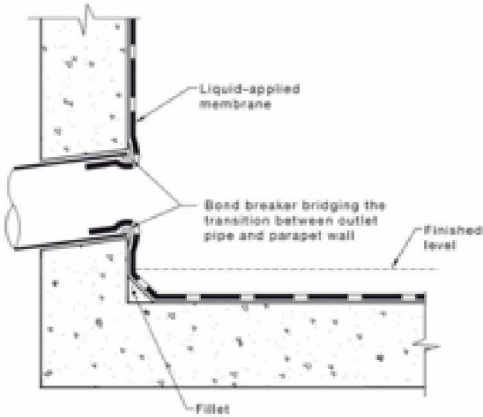

(a) Overflow through parapet

OVERFLOW TO BALCONY:

- SURFACE DRAIN & OVERFLOW TO BALCONY

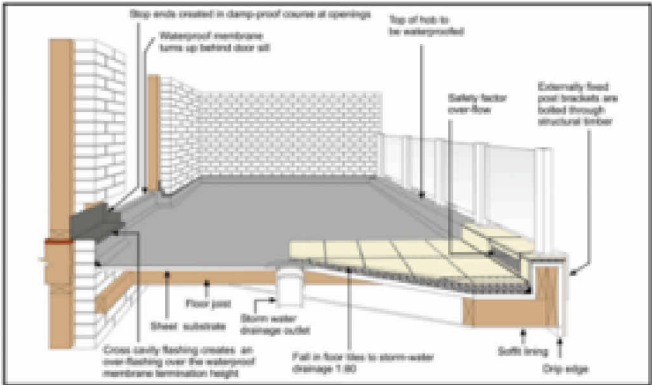

SWIMMING POOL

- PART 12.1.1 (H7D2) OF THE NCC VOLUME 2, AMENDMENT 1 - BUILDING CODE OF AUSTRALIA 2022 & HOUSING PROVISIONS STANDARD 2022
- AS 1926 PART 1-2012 – SWIMMING POOLSAFETY- SAFETY BARRIERS FOR SWIMMING POOLS
- AS 1926 PART 2-2007 - SWIMMING POOL SAFETY- LOCATION OF SAFETY BARRIERS FOR SWIMMING POOLS (INCORPORATING AMENDMENTS 1 AND 2)
- AS 1926 PART 3-2010 – SWIMMING POOL SAFETY- WATER RECIRCULATION SYSTEMS (INCORPORATING AMENDMENT 1)

REV	DATE	DESCRIPTION	BY
2	7-08-2026	CDC ISSUE	



THIS DRAWING IS THE EXCLUSIVE PROPERTY OF THE DEVELOPER & THE REPRODUCTION OF ANY PART WITHOUT THE PRIOR WRITTEN CONSENT OF THE DEVELOPER IS A VIOLATION OF APPLICABLE LAWS. IN NO EVENT SHALL THE DEVELOPER BE HELD LIABLE FOR SPECIAL COLLATERAL, INCIDENTAL OR CONSEQUENTIAL LIABILITY IN CONNECTION WITH THE USE OF THIS DIGITAL DATA ONCE RELEASED FROM THE DEVELOPER'S OFFICE. THIS DRAWING IS TO BE READ & UNDERSTOOD IN CONJUNCTION WITH THE STRUCTURAL, MECHANICAL, ELECTRICAL & / OR ANY OTHER CONSULTANT'S DOCUMENTATION AS MAY BE APPLICABLE TO THE PROJECT PRIOR TO THE START OF ANY WORKS AND FOR ITS DURATION.


PROJECT:
LOT 2322 1 HOPPLES ROAD
1 HOPPLES ROAD MENANGLE PARK

DRAWING TITLE:
GENERAL NOTES

NORTH:


LOT NO: 2322	DATE: 24-09-2026	SCALE: 1 : 2	DRAWING No: CDC.02B	REV: 2
DRAWN BY: AS	CHECKED BY: RH			
DRAFTED BY: SL	CLIENT NAME: Owner			

CDC ISSUE

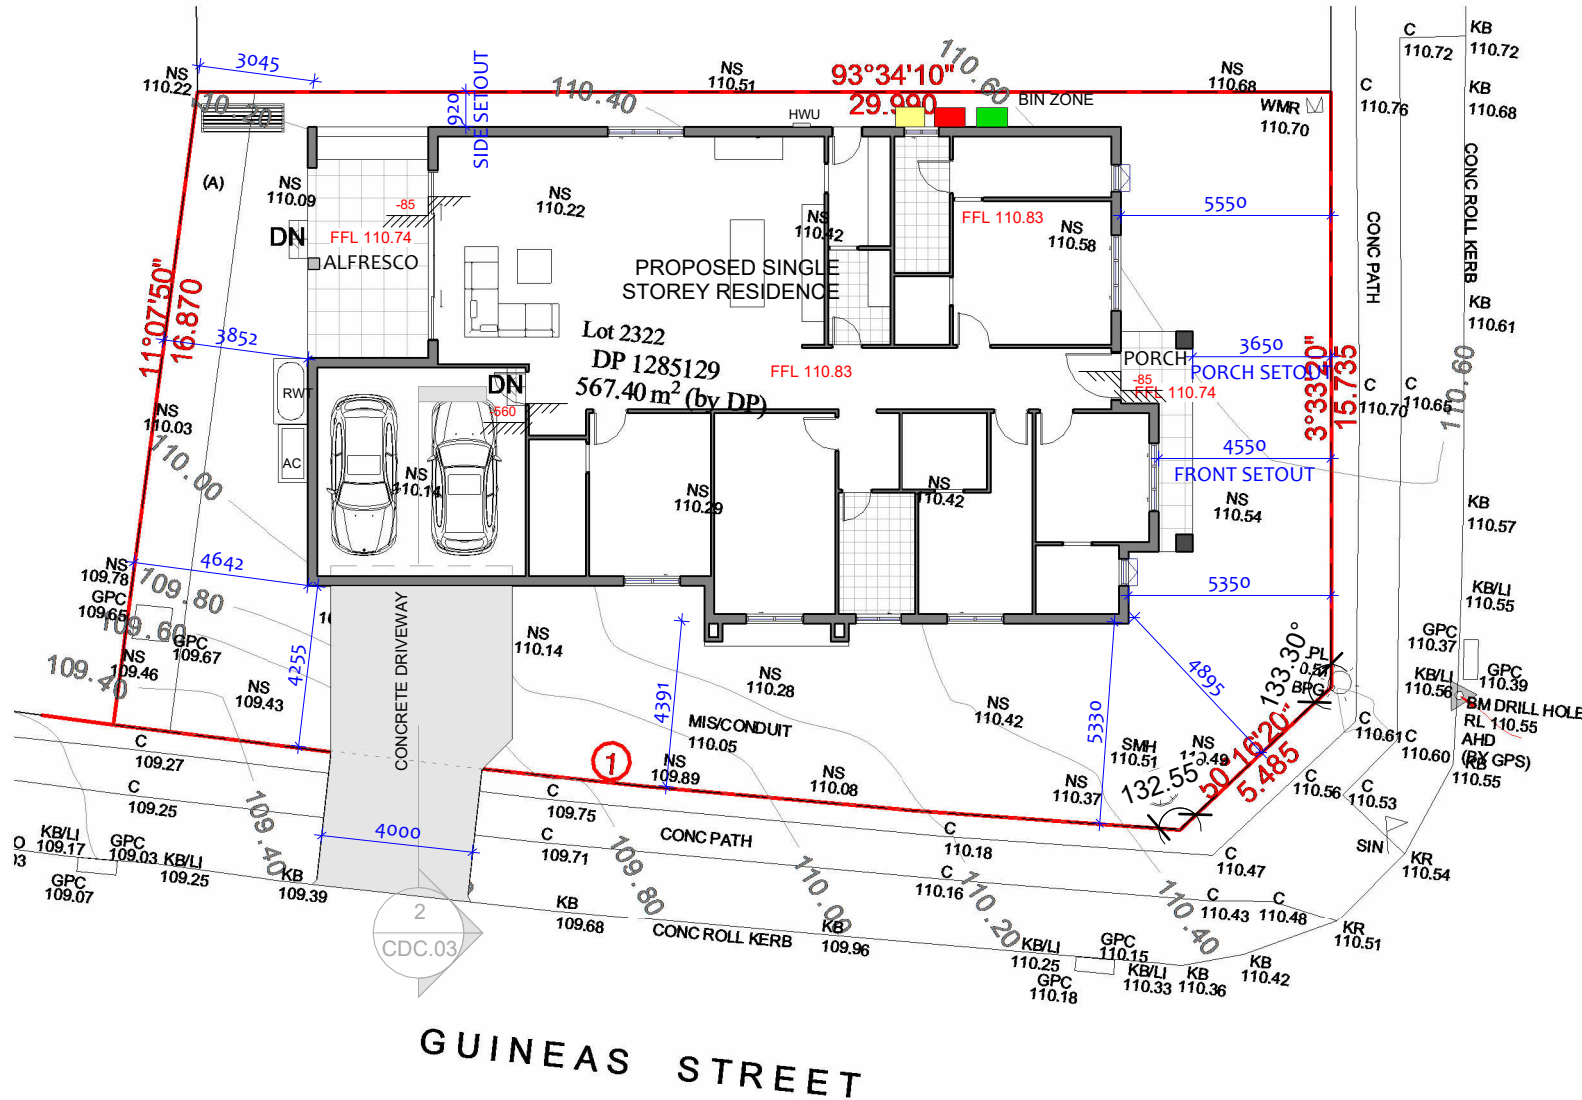

CDC - SITE PLAN

1 : 200

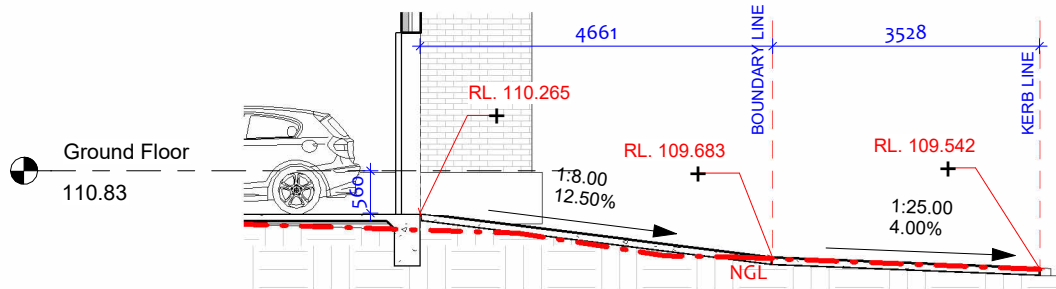

DRIVEWAY SECTION

1 : 100

AREA SCHEDULE (RENTABLE)	
NAME	AREA (m2)
LOT AREA	567.40
GROUND FLOOR	209
FIRST FLOOR	NA
GARAGE	30
STAIRCASE VOID	NA
PRIVATE OPEN SPACE	24
DRIVEWAY	22
FRONT LANDSCAPE	137.5
REAR LANDSCAPE	69.3

GREENFIELD HOUSING CODE COMPLIANCE TABLE

DESCRIPTION		COMPLIANCE		COMMENT
ELEMENT	CODE CONTROL	REQUIREMNT	PROPOSED	
LOAND ZONE	1 GENERAL RESIDENTIAL			
LOT NO	LOT 2322			
LOT AREA	567.40 m2			
LOT WIDTH	Standard Lot Min. 6m at Building Line facing primary road	6.0m	19.45 m	YES
HEIGHT	MAX. Height	8.5m	5.9m (MAX.)	YES
FRONT SETBACK	FRONT SET BACK (Min. Setback from Primary Road) For 300-350 sqm. Lot	4.5 m	4.5m	YES
REAR SET BACK (MIN.)	GROUND FLOOR	3m	3m	YES
	FIRST FLOOR	6m	NA	
SIDE SET BACK (MIN.)	GROUND FLOOR	0.9/2.0m	0.9/4m	YES
	FIRST FLOOR	0.9/2.0m	NA	
FLOOR SPACE RATIO (FSR)	25% of lot area + 150m2	291.85m2	221 m2	YES
GROSS FLOOR AREA PLAN	GROUND FLOOR		209 m2	
	FIRST FLOOR		NA	
TOTAL FLOOR AREA			221 m2	
ROOF AREA			345 m2	
GARAGE			30m2	
PRIVATE OPEN SPACE	>10m Lot width	24m2	24 m2	YES
LANDSCAPE AREA	20 % of TOTAL LAND AREA	113.48 m2	206.8 m2	YES

CDC ISSUE

REV	DATE	DESCRIPTION	BY
2	7-08-2026	CDC ISSUE	

RUBY HOMES

THIS DRAWING IS THE EXCLUSIVE PROPERTY OF THE DEVELOPER & THE REPRODUCTION OF ANY PART WITHOUT THE PRIOR WRITTEN CONSENT OF THE DEVELOPER IS A VIOLATION OF APPLICABLE LAWS. IN NO EVENT SHALL THE DEVELOPER BE HELD LIABLE FOR SPECIAL COLLATERAL, INCIDENTAL OR CONSEQUENTIAL LIABILITY IN CONNECTION WITH THE USE OF THIS DIGITAL DATA ONCE RELEASED FROM THE DEVELOPER'S OFFICE. THIS DRAWING IS TO BE READ & UNDERSTOOD IN CONJUNCTION WITH THE STRUCTURAL, MECHANICAL, ELECTRICAL & / OR ANY OTHER CONSULTANT'S DOCUMENTATION AS MAY BE APPLICABLE TO THE PROJECT PRIOR TO THE START OF ANY WORKS AND FOR ITS DURATION.

PROJECT:
LOT 2322 1 HOPPLES ROAD
1 HOPPLES ROAD MENANGLE PARK

DRAWING TITLE:
LOCATION PLAN AND SITE PLAN



LOT NO: 2322	DATE: 24-09-2026	SCALE: As indicated	DRAWING No: CDC.03	REV: 2
DRAWN BY: AS	CHECKED BY: RH	ISSUED BY:		
DRAFTED BY: SL	CLIENT NAME: Owner			



SD 6-9 GEOTEXTILE INLET FILTER

- 1) FABRICATE A SEDIMENT BARRIER MADE FROM GEOTEXILE.
REFER SD6-7 FOR DETAILS.
- 2) SUPPORT GEOTEXILE WITH MESH TIED TO POSTS AT 1 m Ctrs.
- 3) DO NOT COVER INLET WITH GEOTEXILE.

SD 5-7 STABILISED SITE ACCESS

- 1) STRIP TOPSOIL AND LEVEL SITE.
- 2) COMPACT SUBGRADE.
- 3) COVER AREA WITH GEOTEXILE.
- 4) CONSTRUCT 200 mm THICK PAD OVER GEOTEXILE USING ROADBASE OR 30 mm AGGREGATE. Min 15 m LONG OR TO BUILDING ALIGNMENT. Min 3 m WIDE.
- 5) CONSTRUCT HUMPS IMMEDIATELY WITHIN BOUNDARY TO DIVERT WATER TO A SEDIMENT FENCE OR OTHER SEDIMENT TRAP.

TEMPORARY 1.8M HIGH WIRE MESH
FENCE WITH DUSTPROOF MESH
APPLIED TO FULL HEIGHT TO
BOUNDARIES AS REQUIRED

LOCATION OF WASTE BINS
SEDIMENT FENCE AS REQUIRED
GRAVEL ACCESS
SITE ACCESS AREA TO BE USED FOR
WASHDOWN AREA
FOOTPATH CLEAN AND CLEAR AT ALL
TIMES
LOCATION OF STOCKPILE MATERIAL
MATERIAL STORAGE AREA
TEMPORARY TOILETS
INSTALL TEMPORARY SEDIMENT
BARRIERS TO ALL INLET PITS LIKELY
TO COLLECT SILT LADEN WATER, TO
COUNCIL'S REQUIREMENTS.

SITE WORKS NOTES

1. ORIGIN OF LEVELS PROVIDED BY SURVEYOR
2. THE BUILDER SHALL VERIFY ALL DIMENSIONS AND EXISTING LEVELS ON SITE PRIOR TO THE COMMENCEMENT OF WORK AND ANY DISCREPANCIES SHALL BE REPORTED TO THE SURVEYOR / ENGINEER .
3. TOPSOIL SHALL BE STRIPPED FROM THE CONSTRUCTION AREA AND STOCKPILED ON SITE , TO BE LATER SPREAD OR DISPOSED OFF SITE ,AS DIRECTED BY SUPERVISOR /ENGINEER .
4. ALL THE TRENCH BACKFILL MATERIAL SHALL BE COMPACTED TO THE SAME DENSITY AS THE ADJACENT MATERIAL .
5. ALL SERVICE TRENCHES UNDER VEHICULAR PAVEMENTS SHALL BE BACKFILLED WITH SAND OR APPROVED GRANULAR MATERIALS. TO THE UNDERSIDE OF THE PAVEMENT, AND COMPACTED TO 98% STANDARD MAXIMUM DRY DENSITY ,IN ACCORDANCE WITH AS 1289E1.1.



SEDIMENT AND EROSION NOTES:


- THIS PLAN TO BE READ IN CONJUNCTION WITH SEDIMENT AND EROSION CONTROL DETAILS AS ATTACHED.
 - THE CONTRACTOR SHALL IMPLEMENT ALL SOIL EROSION AND SEDIMENT CONTROL MEASURES AS NECESSARY AND TO THE SATISFACTION OF COUNCIL PRIOR TO THE COMMENCEMENT AND DURING CONSTRUCTION. NO DISTURBANCE TO THE SITE SHALL BE PERMITTED OTHER THAN IN THE IMMEDIATE AREA OF THE WORK AND NO MATERIAL SHALL BE REMOVED FROM THE SITE WITHOUT COUNCIL'S APPROVAL. ALL SEDIMENT AND EROSION CONTROL DEVICES TO BE INSTALLED AND MAINTAINED IN ACCORDANCE WITH STANDARDS OUTLINED IN NSW DEPARTMENT OF HOUSING "MANAGING URBAN STORMWATER-SOILS AND CONSTRUCTIONS".
 - TOPSOIL SHALL BE STRIPPED AND STOCKPILED OUTSIDE HAZARD AREAS SUCH AS DRAINAGE LINES. THIS TOP SOIL IS TO BE RESPIRED LATER ON AREAS TO BE REVEGETATED AND STABILISED ONLY. (I.E ALL FOOTPATHS, BATTERS, SITE REGARDING AREAS, BASINS AND CATCH DRAINS), TOPSOIL SHALL NOT BE RESPIRED ON ANY OTHER AREAS UNLESS SPECIALLY INSTRUCTED BY THE SUPERIDENT. IF THEY ARE TO REMAIN FOR LONGER THAN ONE MONTH STOCKPILES SHALL BE PROTECTED FROM EROSION BY COVERING THEM WITH A MULCH AND HYDROSEEDING AND, IF NECESSARY, BY LOCATING BANKS OR DRAINS DOWNSTREAM OF A STOCKPILE TO RETARD SILT LADEN RUNOFF.
 - THE CONTRACTOR SHALL REGULARLY MAINTAIN ALL SEDIMENT AND EROSION CONTROL DEVICES AND REMOVE ACCUMULATED SILT FROM SUCH DEVICES SUCH THAT MORE THAN 60% OF THEIR CAPACITY NOT LOST. ALL THE SILTS TO BE PLACED OUTSIDE THE LIMIT OF WORKS. THE PERIOD FOR MAINTAINING THESE DEVICES SHALL BE AT LEAST UNTIL ALL DISTURBED AREAS ARE REVEGETATED AND FURTHER AS MAY BE DIRECTED BY THE SUPERINTENDENT OR COUNCIL.
 - LAY TURF STRIP (MIN 300 mm WIDE) ON 100 mm TOPSOIL WITH 1.0 m LONG RETURNS EVERY 6.0m BEHIND ALL KERB AT THE TOP OF ALL BATTERS AND AROUND STRUCTURES IMMEDIATELY AFTER BACKFILLING OR FORMATION.
 - THE CONTRACTOR SHALL GRASS SEED ALL DISTURBED AREAS WITH AN APPROVED MIX AS SHOWN AS PRACTICABLE AFTER COMPLETION OF EARTHWORKS AND REGRADING.
 - VEHICULAR TRAFFIC SHALL BE CONTROLLED DURING CONSTRUCTION CONFINING ACCESS WHERE POSSIBLE TO NOMINATED STABILISED ACCESS POINTS.
 - WHEN ANY DEVICES ARE TO BE HANDED OVER TO COUNCIL, THEY SHALL BE IN CLEAN AND STABLE CONDITION.
- THE CONTRACTOR SHALL IMPLEMENT DUST CONTROL BY REGULAR WETTING DOWN (BUT NOT SATURATING) DISTURBED AREA.
- PROVIDE AND MAINTAIN SILT TRAPS AROUND ALL SURFACE INLET PITS UNTIL CATCHMENT IS REVEGETATED OR PAVED.
- REVEGETATE ALL TRENCHES IMMEDIATELY UPON COMPLETION OF BACKFILLING.
- ALL DRAINAGE PIPE INLETS TO BE CAPPED UNTIL:
- A) DOWNPIPES CONNECTED
 - B) PITS CONSTRUCTED & PROTECTED WITH SILT

CDC ISSUE

PROJECT:
LOT 2322 1 HOPPLES
ROAD
1 HOPPLES ROAD MENANGLE
PARK

DRAWING TITLE:
**SITE ANALYSIS
AND SEDIMENT
CONTROL**

NORTH:

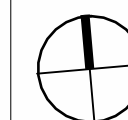


LOT NO: 2322	DATE: 24-09-2026	SCALE:	<u>DRAWING</u> <u>No:</u>	<u>REV:</u> 2
DRAWN BY: AS	CHECKED BY: RH	As indicated	CDC.04	ISSUED BY:
DRAFTED BY: SL	CLIENT NAME: Owner			

BAL – LOW

DESIGNED AS IN ACCORDANCE WITH THE MEASURE AND CONTROLS
CONTAINED WITHIN THE BUSHFIRE ATTACK ASSESSMENT PLAN PREPARED BY
PETERSON BUSHFIRE EXPERT CONSULTING SERVICE PTY, DATED 07-04-2022

2
CDC.10

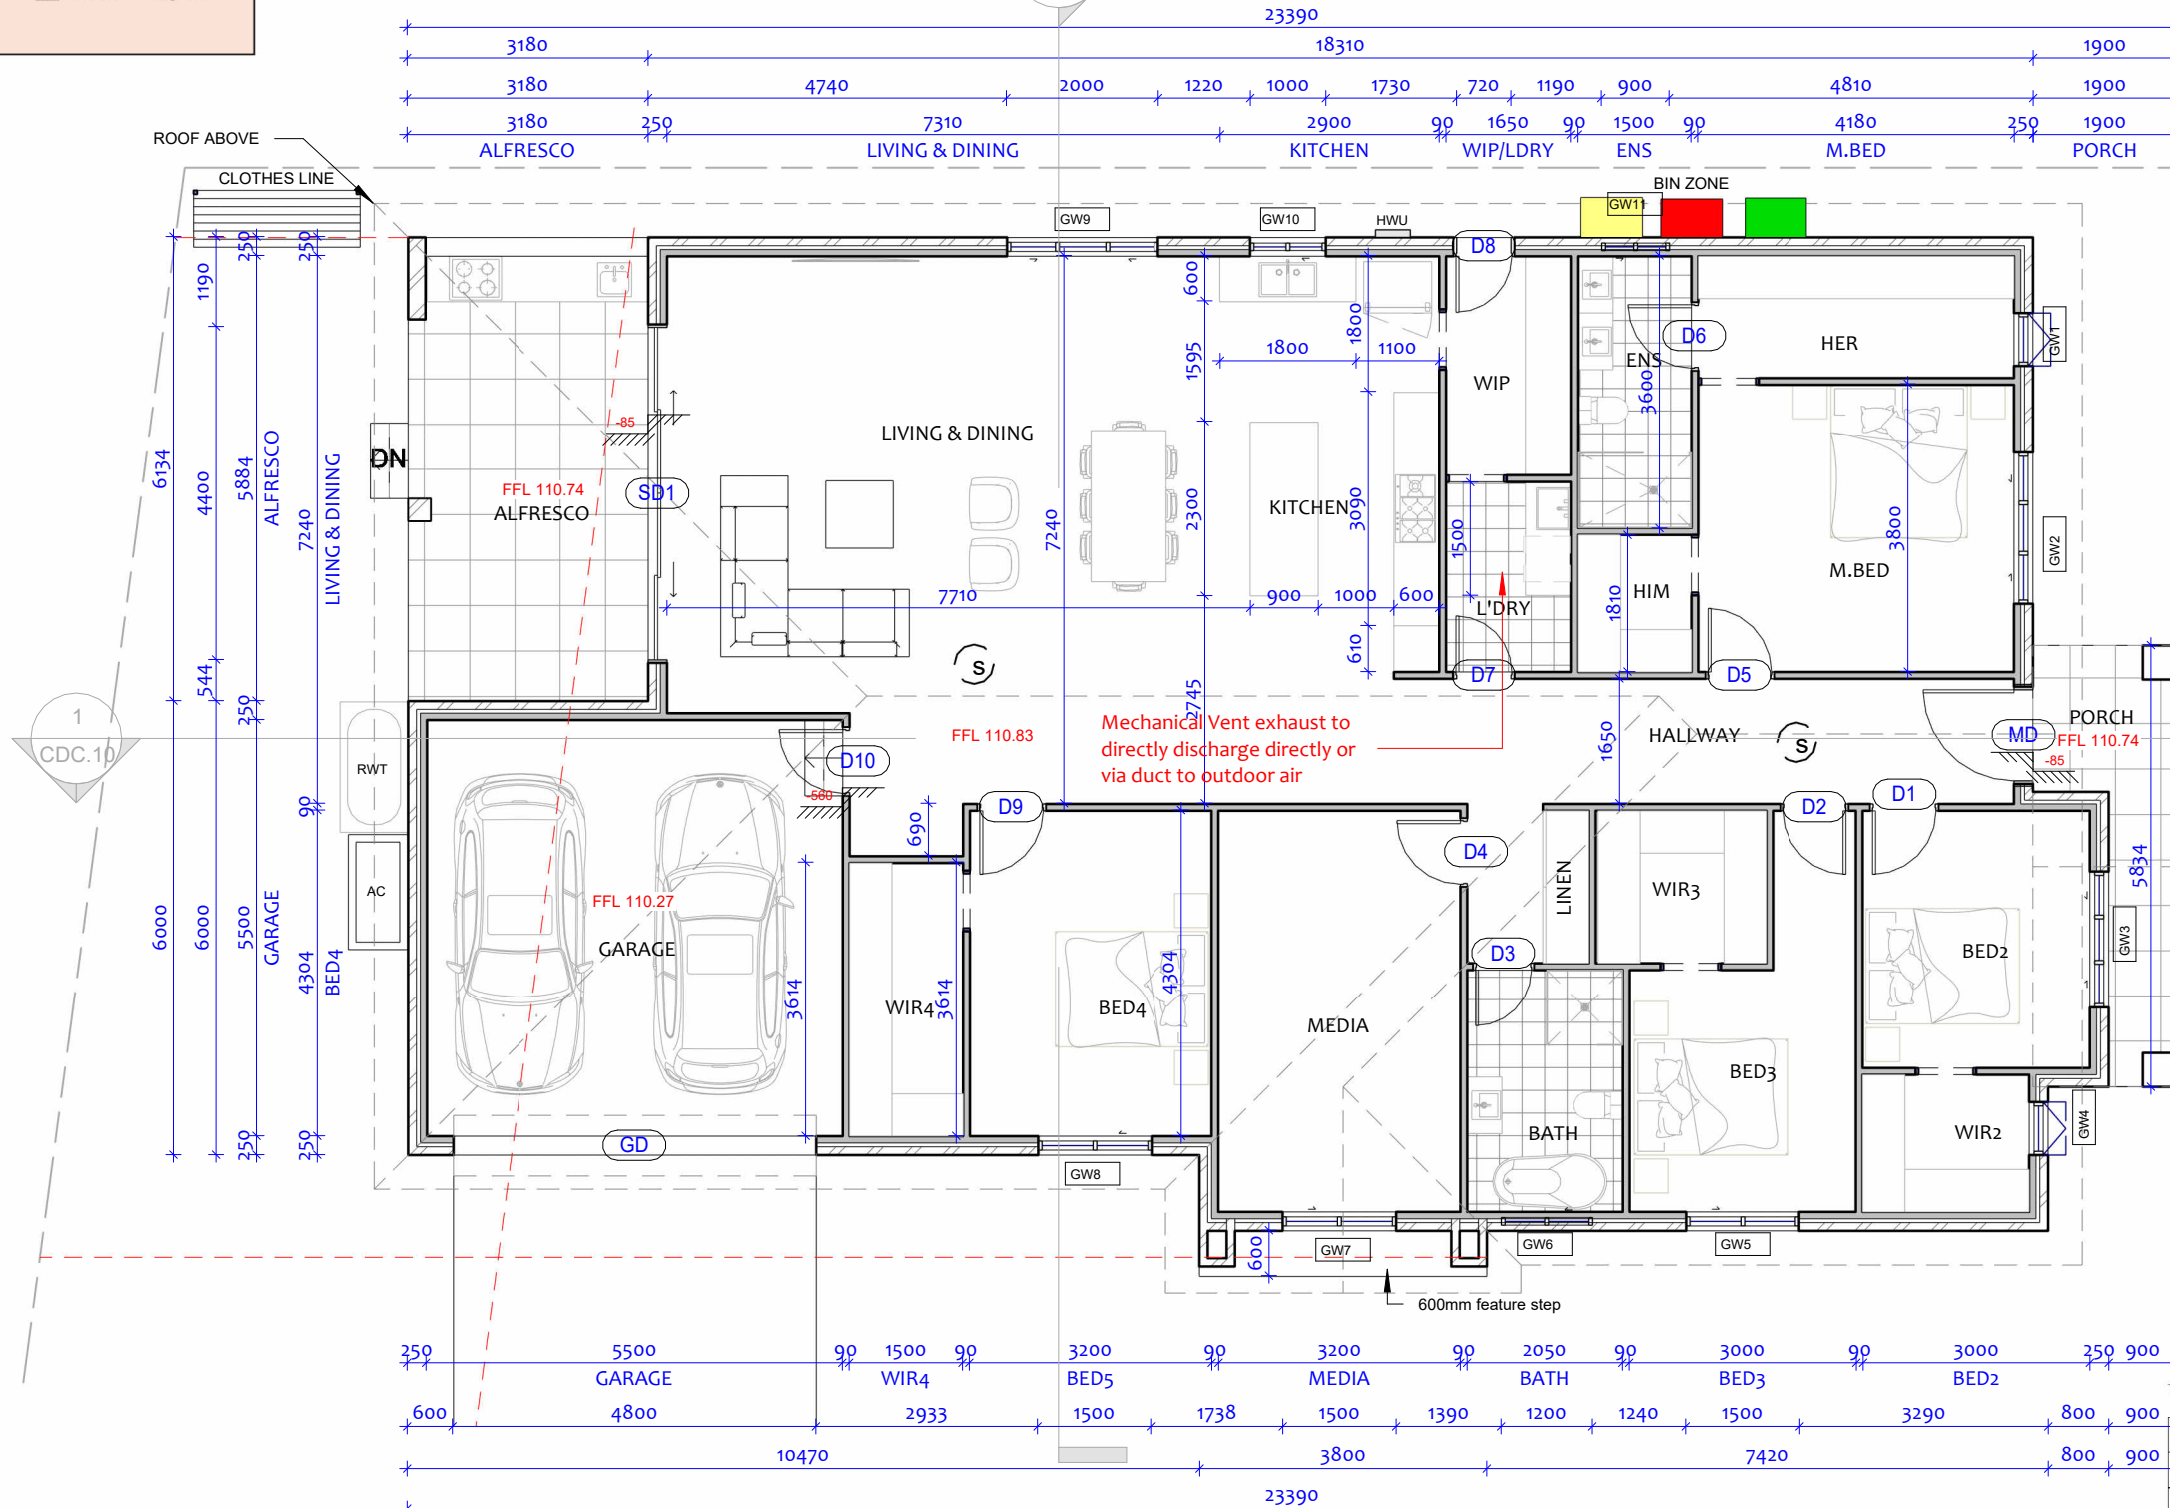

Ground Floor

1 : 100

IMPORTANT NOTES:
ALL DIMENSIONS AND NOTES ON ALL PLANS MUST BE CHECKED AND VERIFIED BY BUILDERS AND OWNER PRIOR TO COMMENCEMENT OF ANY BUILDING WORKS. TO CLARIFY AND CONFIRM WITH CONSTRUCTION COMPANY FOR DISCREPANCIES ON ALL DOCUMENTS AND PLANS PROVIDED FOR CONSTRUCTION. ANY WORK INDICATED ON THE PLAN BUT NOT IN THE SPECIFICATION BUT WHICH IS NECESSARY AS PART OF THE CONTRACT VARIATION TO PLANS. SPECIFICATIONS MAY NOT BE MADE WITHOUT THE WRITTEN CONSENT OF OWNER. IT IS THE RESPONSIBILITY OF THE BUILDER/END USER TO VERIFY PLANS AND SPECIFICATIONS AS TO THEIR ACCURACY AND COMPLY CURRENT BCA AND AUSTRALIAN STANDARDS. WINDOWS TO COMPLY WITH 3.9.3.5 OF THE BCA.

THE FINISHED ROOM SIZE WILL VARY DEPENDING ON GYPROCK THICKNESS, WALL FINISH I.E TILES AND GLUE, BEDDING HEIGHTS, SKIRTING INSTALLATION.

THE MEASUREMENTS GIVEN IS STRUCTURAL SIZES ONLY NOT FINISHED FLOOR SIZE.

Table 12: Guide performance for typical Building Façade Treatments for Noise Affected Lots⁷

Building Component	Acoustic Rating Required	Indicative Requirements/Construction
Glazing	R _w 24-35	4mm float up to 10.38mm laminate glass with acoustic seals
Walls	R _w 40-45	Standard masonry or brick veneer OR Upgraded lightweight constructions
Roof/ceiling	R _w 40-42	Pitched sheet metal roof with Anticon insulation blanket, R2.5-R3.5 ceiling insulation, 10mm plasterboard ceiling. OR Pitched tiled roof with sarking, R2.5-R3.5 ceiling insulation, 10mm plasterboard ceiling.

NOTE: PLEASE REFER TO TENDER FOR ALL INCLUSIONS.


REV	DATE	DESCRIPTION	BY
2	7-08-2026	CDC ISSUE	
1	10-07-2026	New Concept Plan	

RUBY HOMES

THIS DRAWING IS THE EXCLUSIVE PROPERTY OF THE DEVELOPER & THE REPRODUCTION OF ANY PART WITHOUT THE PRIOR WRITTEN CONSENT OF THE DEVELOPER IS A VIOLATION OF APPLICABLE LAWS. IN NO EVENT SHALL THE DEVELOPER BE HELD LIABLE FOR SPECIAL COLLATERAL, INCIDENTAL OR CONSEQUENTIAL LIABILITY IN CONNECTION WITH THE USE OF THIS DIGITAL DATA ONCE RELEASED FROM THE DEVELOPER'S OFFICE. THIS DRAWING IS TO BE READ & UNDERSTOOD IN CONJUNCTION WITH THE STRUCTURAL, MECHANICAL, ELECTRICAL & / OR ANY OTHER CONSULTANT'S DOCUMENTATION AS MAY BE APPLICABLE TO THE PROJECT PRIOR TO THE START OF ANY WORKS AND FOR ITS DURATION.

PROJECT:
LOT 2322 1 HOPPLES ROAD
1 HOPPLES ROAD MENANGLE PARK

DRAWING TITLE:
GROUND FLOOR PLAN

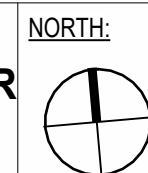


LOT NO: 2322	DATE: 24-09-2026	SCALE: 1 : 100	DRAWING No: CDC.05	REV: 2
DRAWN BY: AS	CHECKED BY: RH	ISSUED BY:		
DRAFTED BY: SL	CLIENT NAME: Owner			

☒ BAL – LOW

DESIGNED AS IN ACCORDANCE WITH THE MEASURE AND CONTROLS
CONTAINED WITHIN THE BUSHFIRE ATTACK ASSESSMENT PLAN PREPARED BY
PETERSON BUSHFIRE EXPERT CONSULTING SERVICE PTY, DATED 07-04-2022

2
CDC.10

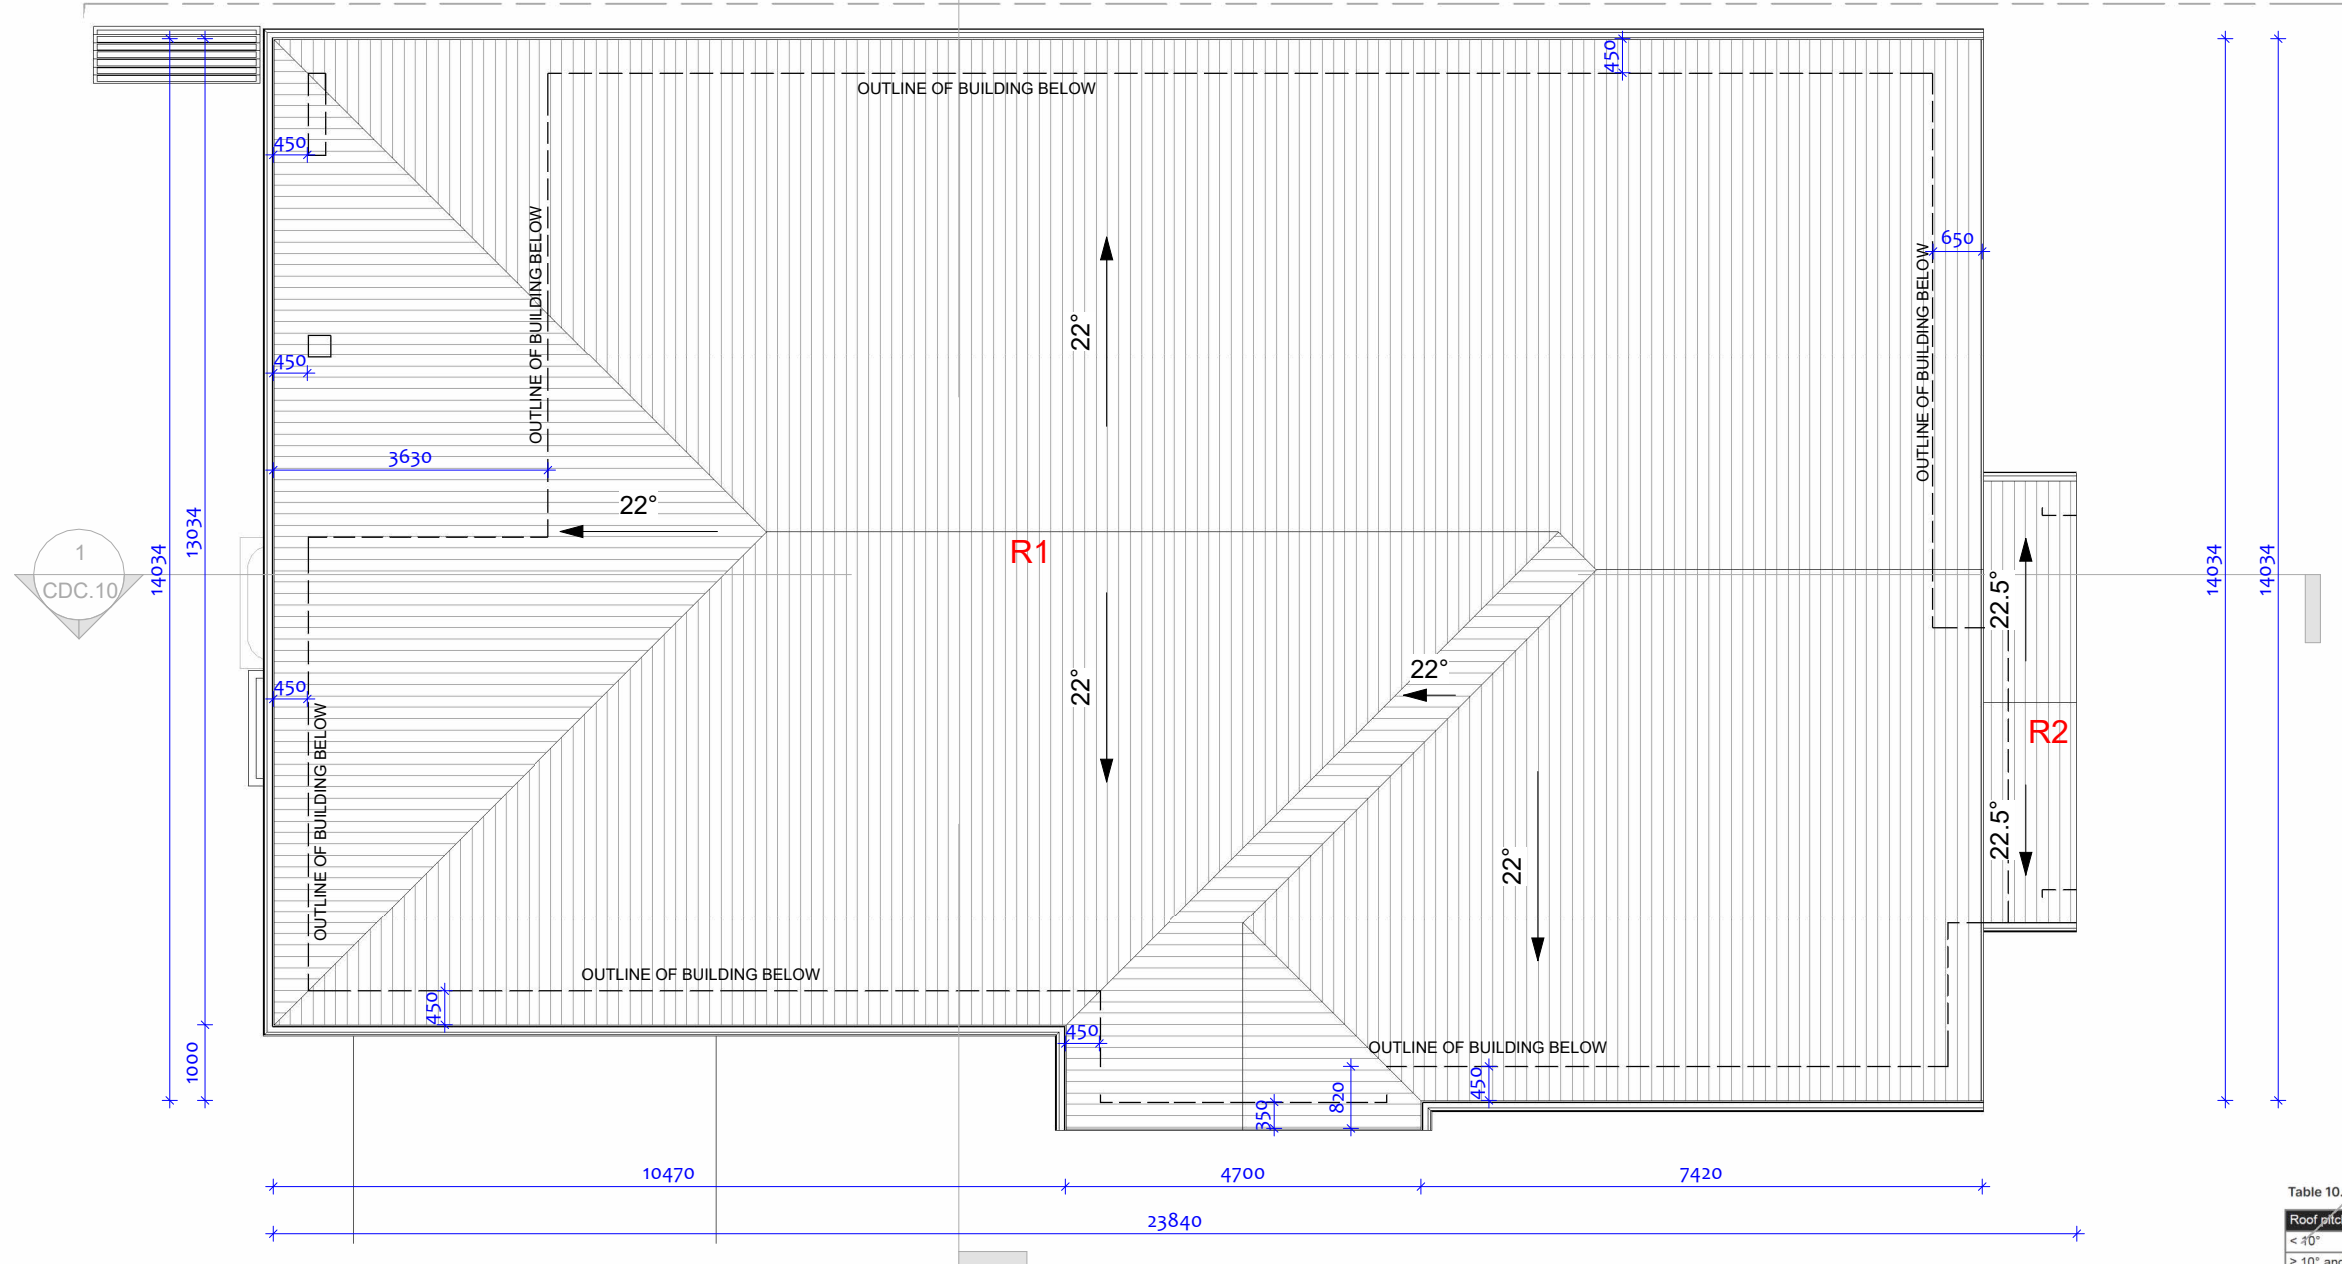

ROOF PLAN

1 : 100

NOTE: PLEASE REFER TO TENDER FOR ALL INCLUSIONS.

Figure 10.8.3 (explanatory): Example of roof space with low level ventilation

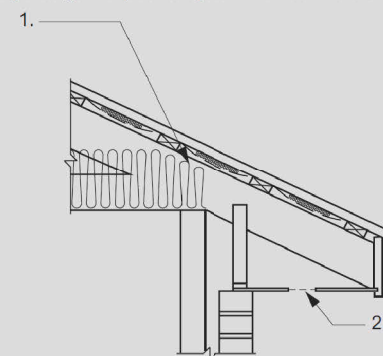


Figure Notes

- (1) Minimum 20 mm gap maintained between insulation and sarking.
(2) Eave ventilation opening in accordance with Table 10.8.3.

IMPORTANT NOTES:
ALL DIMENSIONS AND NOTES ON ALL PLANS MUST BE CHECKED AND VERIFIED BY BUILDERS AND OWNER PRIOR TO COMMENCEMENT OF ANY BUILDING WORKS. TO CLARIFY AND CONFIRM WITH CONSTRUCTION COMPANY FOR DISCREPANCIES ON ALL DOCUMENTS AND PLANS PROVIDED FOR CONSTRUCTION. ANY WORK INDICATED ON THE PLAN BUT NOT IN THE SPECIFICATION BUT WHICH IS NECESSARY AS PART OF THE CONTRACT VARIATION TO PLANS. SPECIFICATIONS MAY NOT BE MADE WITHOUT THE WRITTEN CONSENT OF OWNER. IT IS THE RESPONSIBILITY OF THE BUILDER/END USER TO VERIFY PLANS AND SPECIFICATIONS AS TO THEIR ACCURACY AND COMPLY CURRENT BCA AND AUSTRALIAN STANDARDS. WINDOWS TO COMPLY WITH 3.9.3.5 OF THE BCA.

THE FINISHED ROOM SIZE WILL VARY DEPENDING ON GYPROCK THICKNESS, WALL FINISH I.E TILES AND GLUE, BEDDING HEIGHTS, SKIRTING INSTALLATION.

THE MEASUREMENTS GIVEN IS STRUCTURAL SIZES ONLY NOT FINISHED FLOOR SIZE.

ABCB HOUSING PROVISIONS STANDARD 2022

10.8.3 VENTILATION OF ROOF SPACES

1. IN CLIMATE ZONES 6,7 AND 8, A ROOF MUST HAVE A ROOF SPACE THAT (A) IS LOCATED

(I) IMMEDIATELY ABOVE THE PRIMARY INSULATION LAYER, OR
(II) IMMEDIATELY ABOVE SARKING WITH A VAPOUR PERMEANCE OF NOT LESS THAN 1.14 µG/N.S. WHICH IMMEDIATELY ABOVE THE PRIMARY INSULATION LAYER, OR
(III) IMMEDIATELY ABOVE CEILING INSULATION THAT MEETS THE REQUIREMENTS OF 13.2.3(3) AND 13.2.3(4); AND
(B) HAS A HEIGHT OF NOT LESS THAN 20MM; AND
(C) IS EITHER -

TABLE
(I) VENTILATED TO OUTDOOR AIR THROUGH EVENLY DISTRIBUTED OPENINGS IN ACCORDANCE WITH 10.8.3; OR
(II) LOCATED IMMEDIATELY UNDERNEATH THE ROOF TILES OF A UNSARKED TILED ROOF.

Table 10.8.3: Roof space ventilation requirements

Roof pitch	Ventilation openings
< 4°	25,000 mm ² /m provided at each of two opposing ends
≥ 10° and < 15°	25,000 mm ² /m provided at the eaves and 5,000 mm ² /m at high level
≥ 15° and < 75°	7,000 mm ² /m provided at the eaves and 5,000 mm ² /m at high level, plus an additional 18,000 mm ² /m at the eaves if the roof has a cathedral ceiling

Roof Schedule

Mark	Area	Comments
R1	333 m ²	COLORBOND
R2	12 m ²	COLORBOND

Ground Ceiling: 2 344 m²

CDC ISSUE


REV	DATE	DESCRIPTION	BY
2	7-08-2026	CDC ISSUE	

RUBY HOMES


THIS DRAWING IS THE EXCLUSIVE PROPERTY OF THE DEVELOPER & THE REPRODUCTION OF ANY PART WITHOUT THE PRIOR WRITTEN CONSENT OF THE DEVELOPER IS A VIOLATION OF APPLICABLE LAWS. IN NO EVENT SHALL THE DEVELOPER BE HELD LIABLE FOR SPECIAL COLLATERAL, INCIDENTAL OR CONSEQUENTIAL LIABILITY IN CONNECTION WITH THE USE OF THIS DIGITAL DATA ONCE RELEASED FROM THE DEVELOPER'S OFFICE. THIS DRAWING IS TO BE READ & UNDERSTOOD IN CONJUNCTION WITH THE STRUCTURAL, MECHANICAL, ELECTRICAL & / OR ANY OTHER CONSULTANT'S DOCUMENTATION AS MAY BE APPLICABLE TO THE PROJECT PRIOR TO THE START OF ANY WORKS AND FOR ITS DURATION.

PROJECT:
LOT 2322 1 HOPPLES ROAD
1 HOPPLES ROAD MENANGLE PARK


DRAWING TITLE:
ROOF PLAN

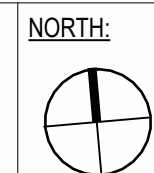

LOT NO:	DATE:	SCALE:	DRAWING No:	REV:
2322	24-09-2026	1 : 100	CDC.07	2
DRAWN BY:	CHECKED BY:			
AS	RH			
DRAFTED BY:	CLIENT NAME:			
SL	Owner			

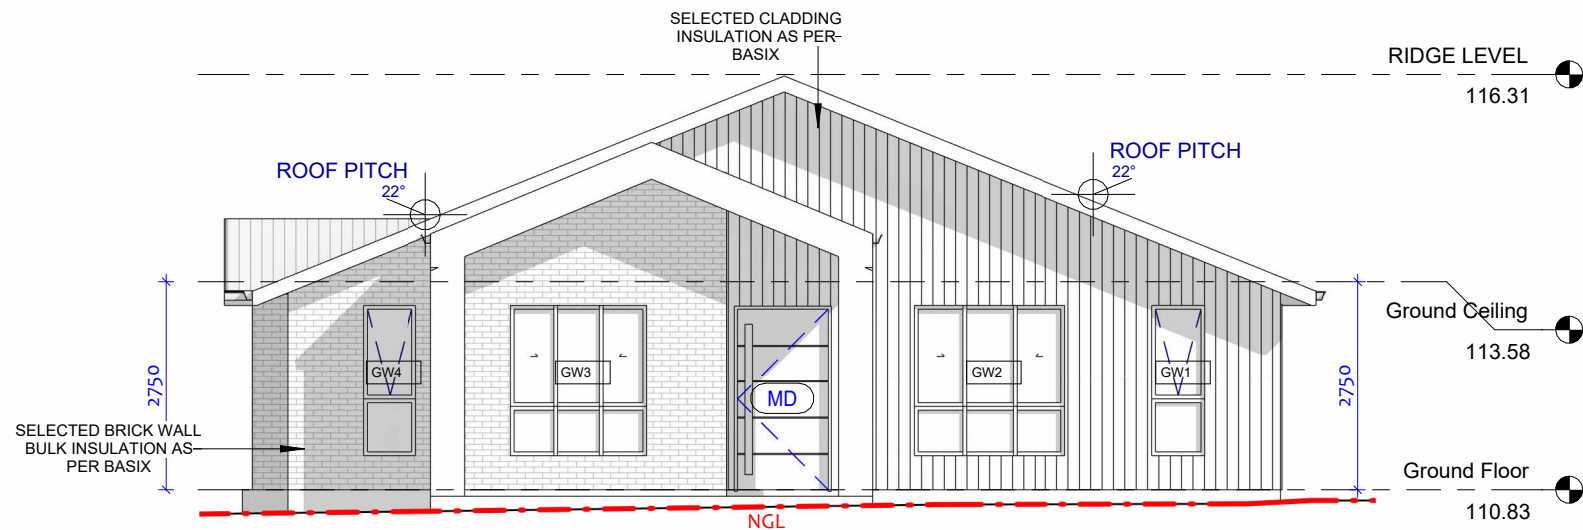

1 EAST Elevation
1 : 100

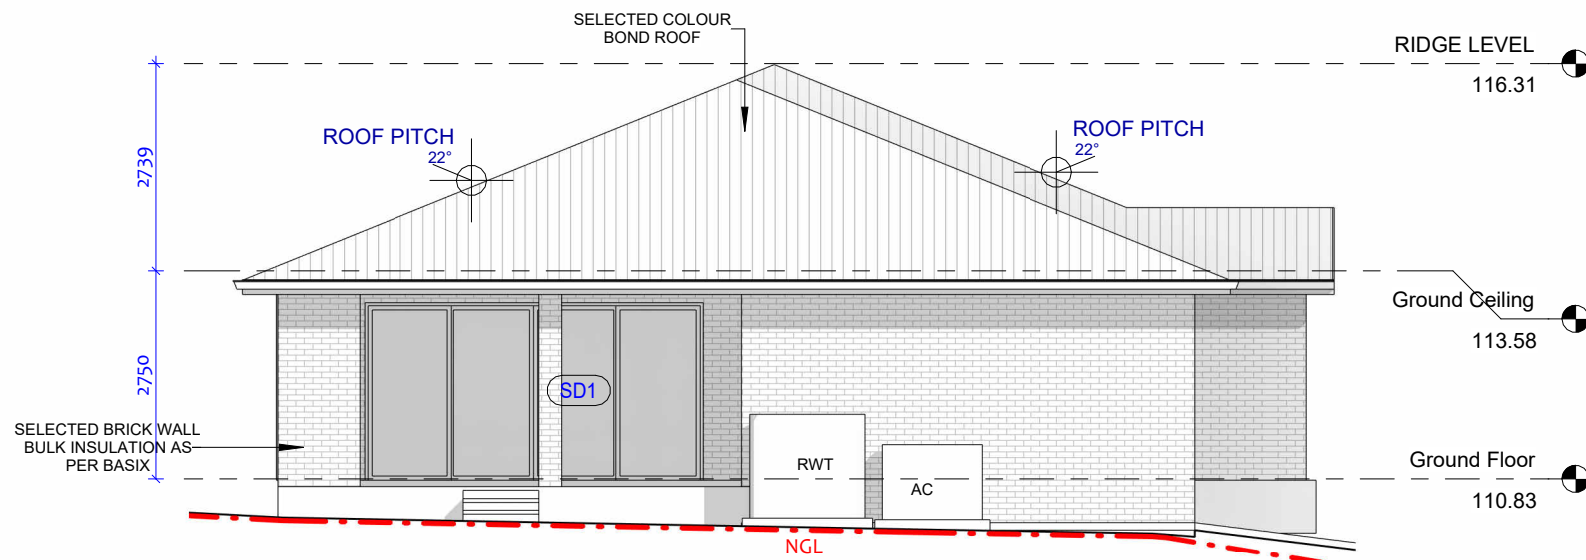

2 WEST Elevation
1 : 100

Window Schedule 1					
Mark	Height	Width	Sill Height	Head Height	Description

Ground Floor

GW1	2000	700	450	2450	FIXED with AWNING
GW2	2000	2000	450	2450	SLIDING & FIXED
GW3	2000	1800	450	2450	SLIDING & FIXED
GW4	2000	700	450	2450	FIXED with AWNING
GW5	2000	1500	450	2450	SLIDING
GW6	800	1200	1650	2450	SLIDING
GW7	2000	1500	450	2450	SLIDING
GW8	2000	1500	450	2450	SLIDING
GW9	2000	2000	450	2450	SLIDING & FIXED
GW10	600	1000	1000	1600	SLIDING
GW11	800	900	1650	2450	SLIDING

Ground Floor: 11

Door Schedule 1				
Mark	Height	Width	Count	Description

Ground Floor

D1	2340	820	1	FLUSH DOOR
D2	2340	820	1	FLUSH DOOR
D3	2340	720	1	FLUSH DOOR
D4	2340	820	1	FLUSH DOOR
D5	2340	820	1	FLUSH DOOR
D6	2340	820	1	FLUSH DOOR
D7	2340	720	1	FLUSH DOOR
D8	2340	720	1	FLUSH DOOR
D9	2340	820	1	FLUSH DOOR
D10	2340	820	1	FLUSH DOOR
GD	2400	4800	1	GARAGE DOOR
MD	2400	1200	1	SOLID CORE DOOR
SD1	2300	4400	1	SLIDING DOOR

Ground Floor: 13

				CDC ISSUE			
				LOT NO:	DATE:	SCALE:	DRAWING No:
				2322	24-09-2026		
				DRAWN BY:	CHECKED BY:		
				AS	RH		
				DRAFTED BY:	CLIENT NAME:		
				SL	Owner		
2	7-08-2026	CDC ISSUE					
REV	DATE	DESCRIPTION	BY				



THIS DRAWING IS THE EXCLUSIVE PROPERTY OF THE DEVELOPER & THE REPRODUCTION OF ANY PART WITHOUT THE PRIOR WRITTEN CONSENT OF THE DEVELOPER IS A VIOLATION OF APPLICABLE LAWS. IN NO EVENT SHALL THE DEVELOPER BE HELD LIABLE FOR SPECIAL COLLATERAL, INCIDENTAL OR CONSEQUENTIAL LIABILITY IN CONNECTION WITH THE USE OF THIS DIGITAL DATA ONCE RELEASED FROM THE DEVELOPER'S OFFICE. THIS DRAWING IS TO BE READ & UNDERSTOOD IN CONJUNCTION WITH THE STRUCTURAL, MECHANICAL, ELECTRICAL & / OR ANY OTHER CONSULTANT'S DOCUMENTATION AS MAY BE APPLICABLE TO THE PROJECT PRIOR TO THE START OF ANY WORKS AND FOR ITS DURATION.

PROJECT:

LOT 2322 1 HOPPLES ROAD

1 HOPPLES ROAD MENANGLE PARK

DRAWING TITLE:

ELEVATION 01

NORTH:



LOT NO:

2322

DATE:

24-09-2026

SCALE:

1 : 100


DRAWING No:

CDC.08


REV:

2

ISSUED BY:

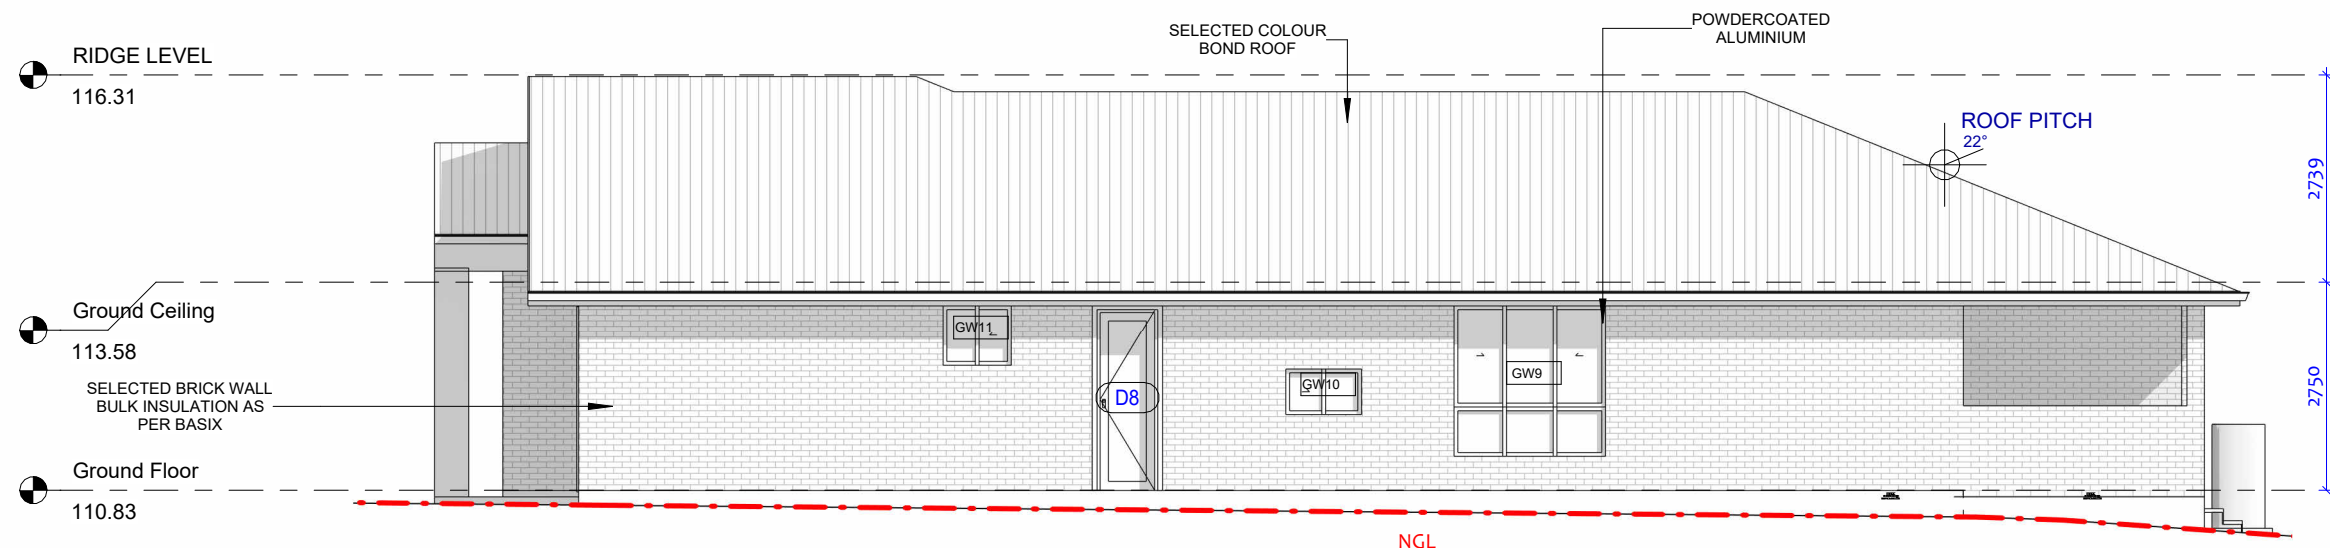

1 NORTH Elevation
1 : 100

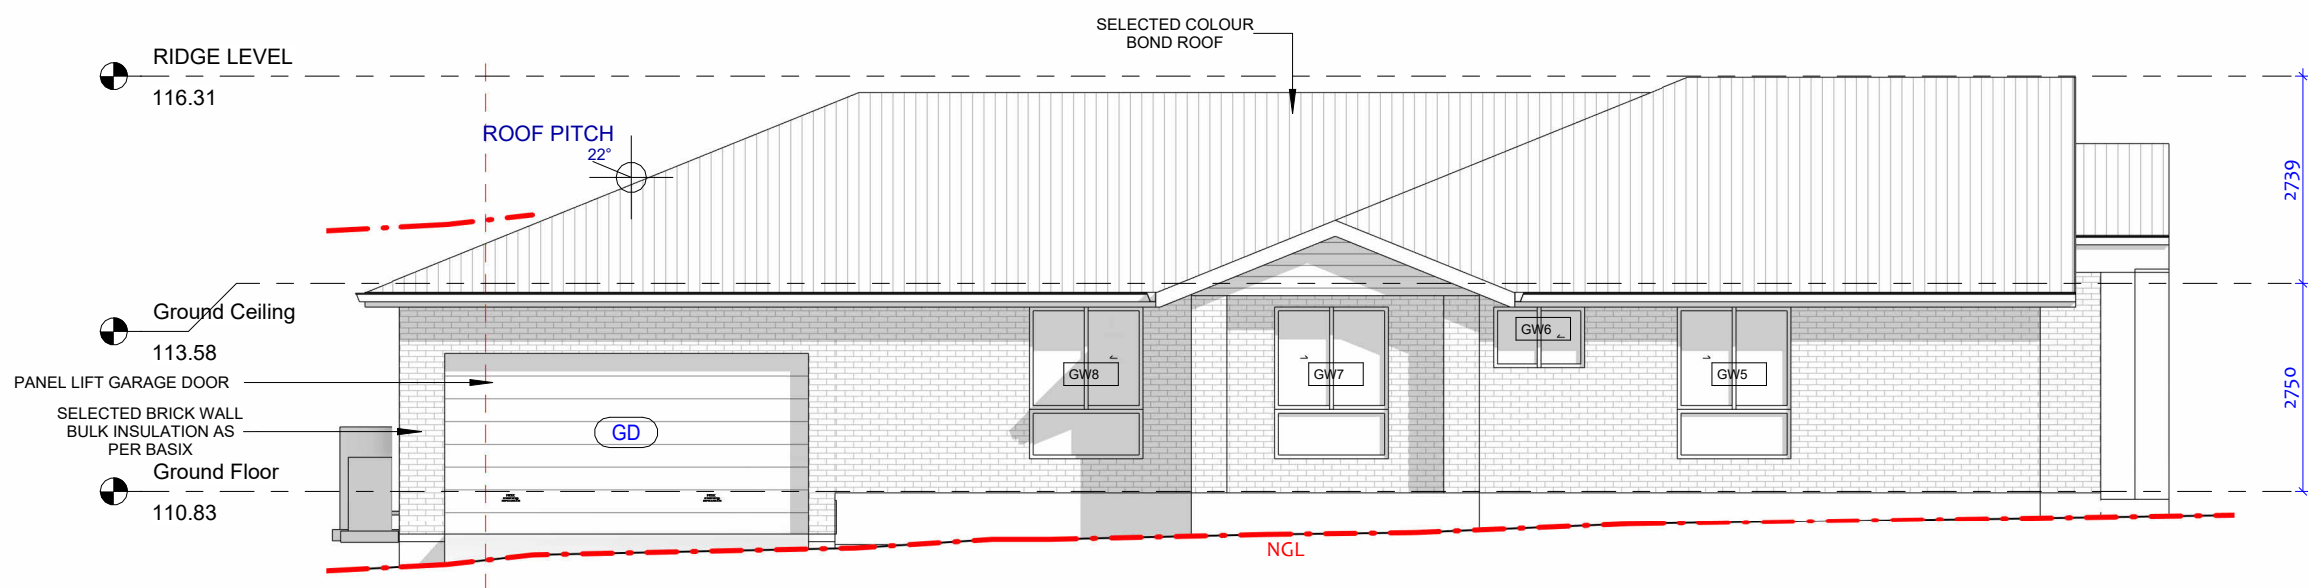

2 SOUTH Elevation
1 : 100

REV	DATE	DESCRIPTION	BY
2	7-08-2026	CDC ISSUE	



THIS DRAWING IS THE EXCLUSIVE PROPERTY OF THE DEVELOPER & THE REPRODUCTION OF ANY PART WITHOUT THE PRIOR WRITTEN CONSENT OF THE DEVELOPER IS A VIOLATION OF APPLICABLE LAWS. IN NO EVENT SHALL THE DEVELOPER BE HELD LIABLE FOR SPECIAL COLLATERAL, INCIDENTAL OR CONSEQUENTIAL LIABILITY IN CONNECTION WITH THE USE OF THIS DIGITAL DATA ONCE RELEASED FROM THE DEVELOPER'S OFFICE. THIS DRAWING IS TO BE READ & UNDERSTOOD IN CONJUNCTION WITH THE STRUCTURAL, MECHANICAL, ELECTRICAL & / OR ANY OTHER CONSULTANT'S DOCUMENTATION AS MAY BE APPLICABLE TO THE PROJECT PRIOR TO THE START OF ANY WORKS AND FOR ITS DURATION.

PROJECT:
LOT 2322 1 HOPPLES ROAD
1 HOPPLES ROAD MENANGLE PARK

DRAWING TITLE:
ELEVATION 02

NORTH:


LOT NO:
2322
DRAWN BY:
AS
DRAFTED BY:
SL

DATE:
24-09-2026
CHECKED BY:
RH
CLIENT NAME:
Owner


SCALE:
1 : 100

CDC ISSUE

DRAWING No:
REV:
2
ISSUED BY:

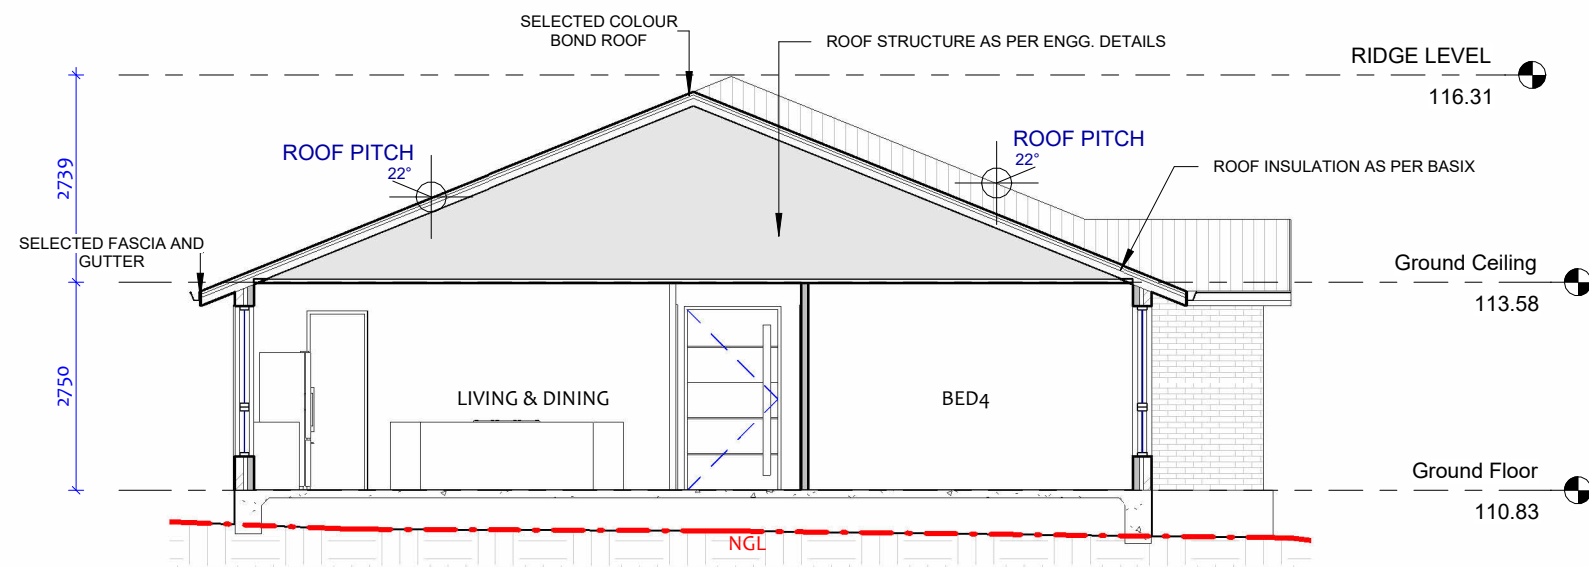

2 CROSS SECTION
1 : 100

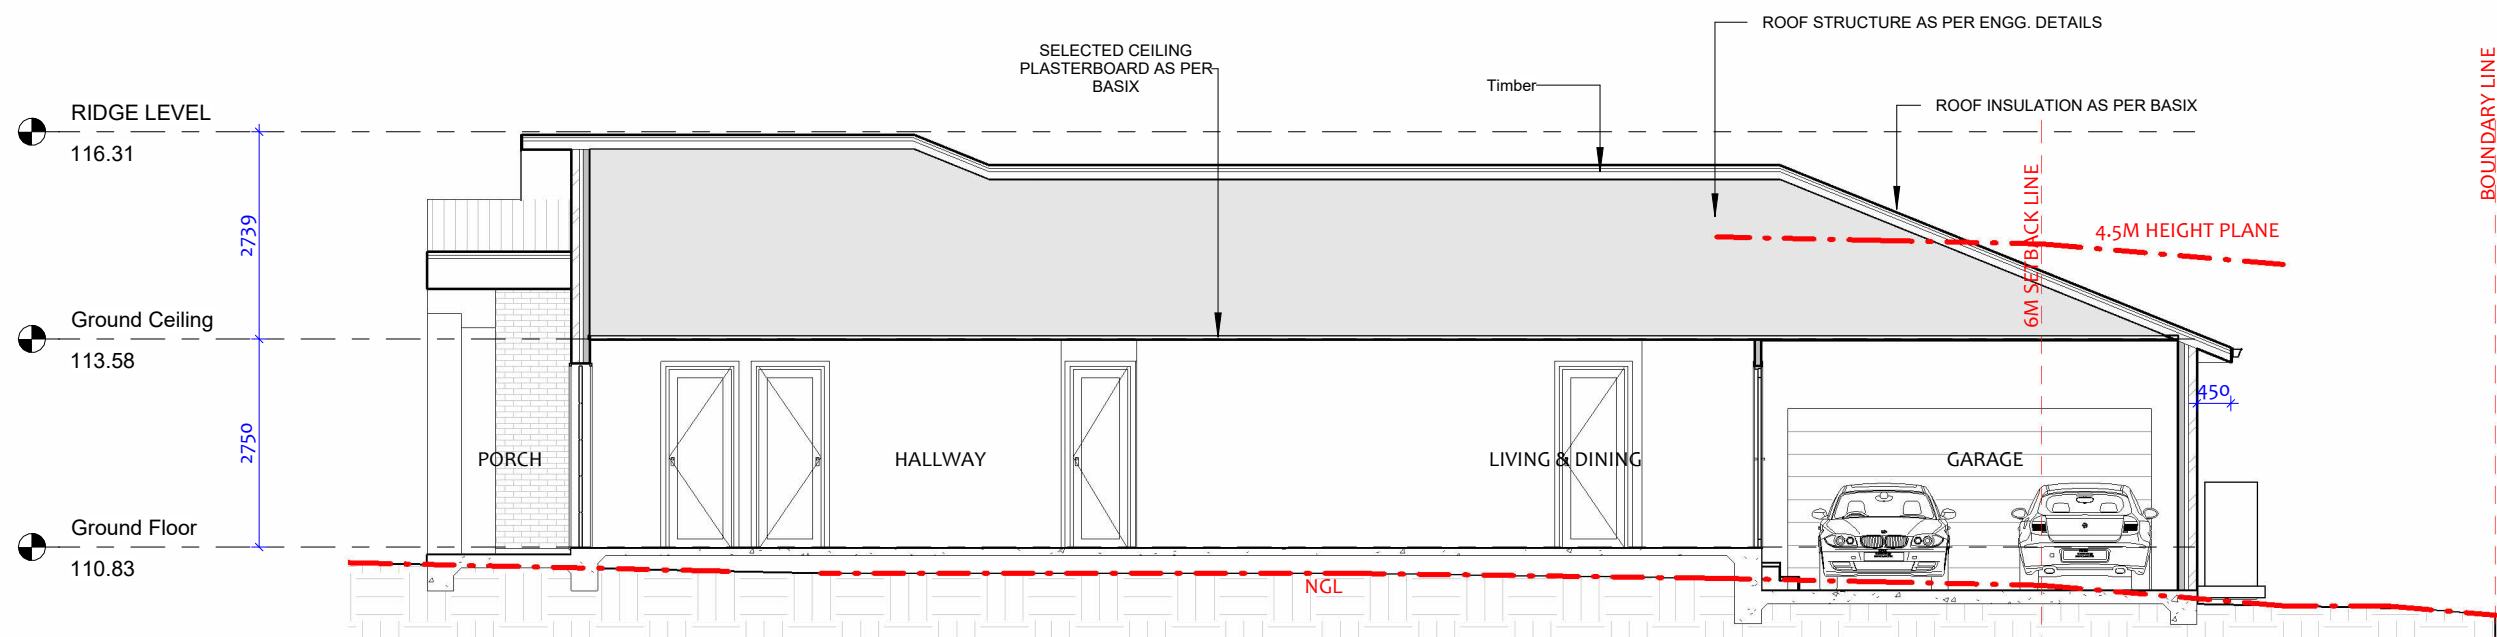

1 LONGITUDINAL SECTION
1 : 100

REV	DATE	DESCRIPTION	BY
2	7-08-2026	CDC ISSUE	



RUBY

 HOMES

THIS DRAWING IS THE EXCLUSIVE PROPERTY OF THE DEVELOPER & THE REPRODUCTION OF ANY PART WITHOUT THE PRIOR WRITTEN CONSENT OF THE DEVELOPER IS A VIOLATION OF APPLICABLE LAWS. IN NO EVENT SHALL THE DEVELOPER BE HELD LIABLE FOR SPECIAL COLLATERAL, INCIDENTAL OR CONSEQUENTIAL LIABILITY IN CONNECTION WITH THE USE OF THIS DIGITAL DATA ONCE RELEASED FROM THE DEVELOPER'S OFFICE. THIS DRAWING IS TO BE READ & UNDERSTOOD IN CONJUNCTION WITH THE STRUCTURAL, MECHANICAL, ELECTRICAL & / OR ANY OTHER CONSULTANT'S DOCUMENTATION AS MAY BE APPLICABLE TO THE PROJECT PRIOR TO THE START OF ANY WORKS AND FOR ITS DURATION.

PROJECT:
LOT 2322 1 HOPPLES ROAD
1 HOPPLES ROAD MENANGLE PARK

DRAWING TITLE:
SECTIONS

NORTH:


LOT NO:
 2322
 DRAWN BY:
 AS
 DRAFTED BY:
 SL

DATE:
 24-09-2026
 CHECKED BY:
 RH
 CLIENT NAME:
 Owner

SCALE:
 1 : 100

CDC ISSUE

DRAWING No:
 CDC.10
 REV: 2
 ISSUED BY:

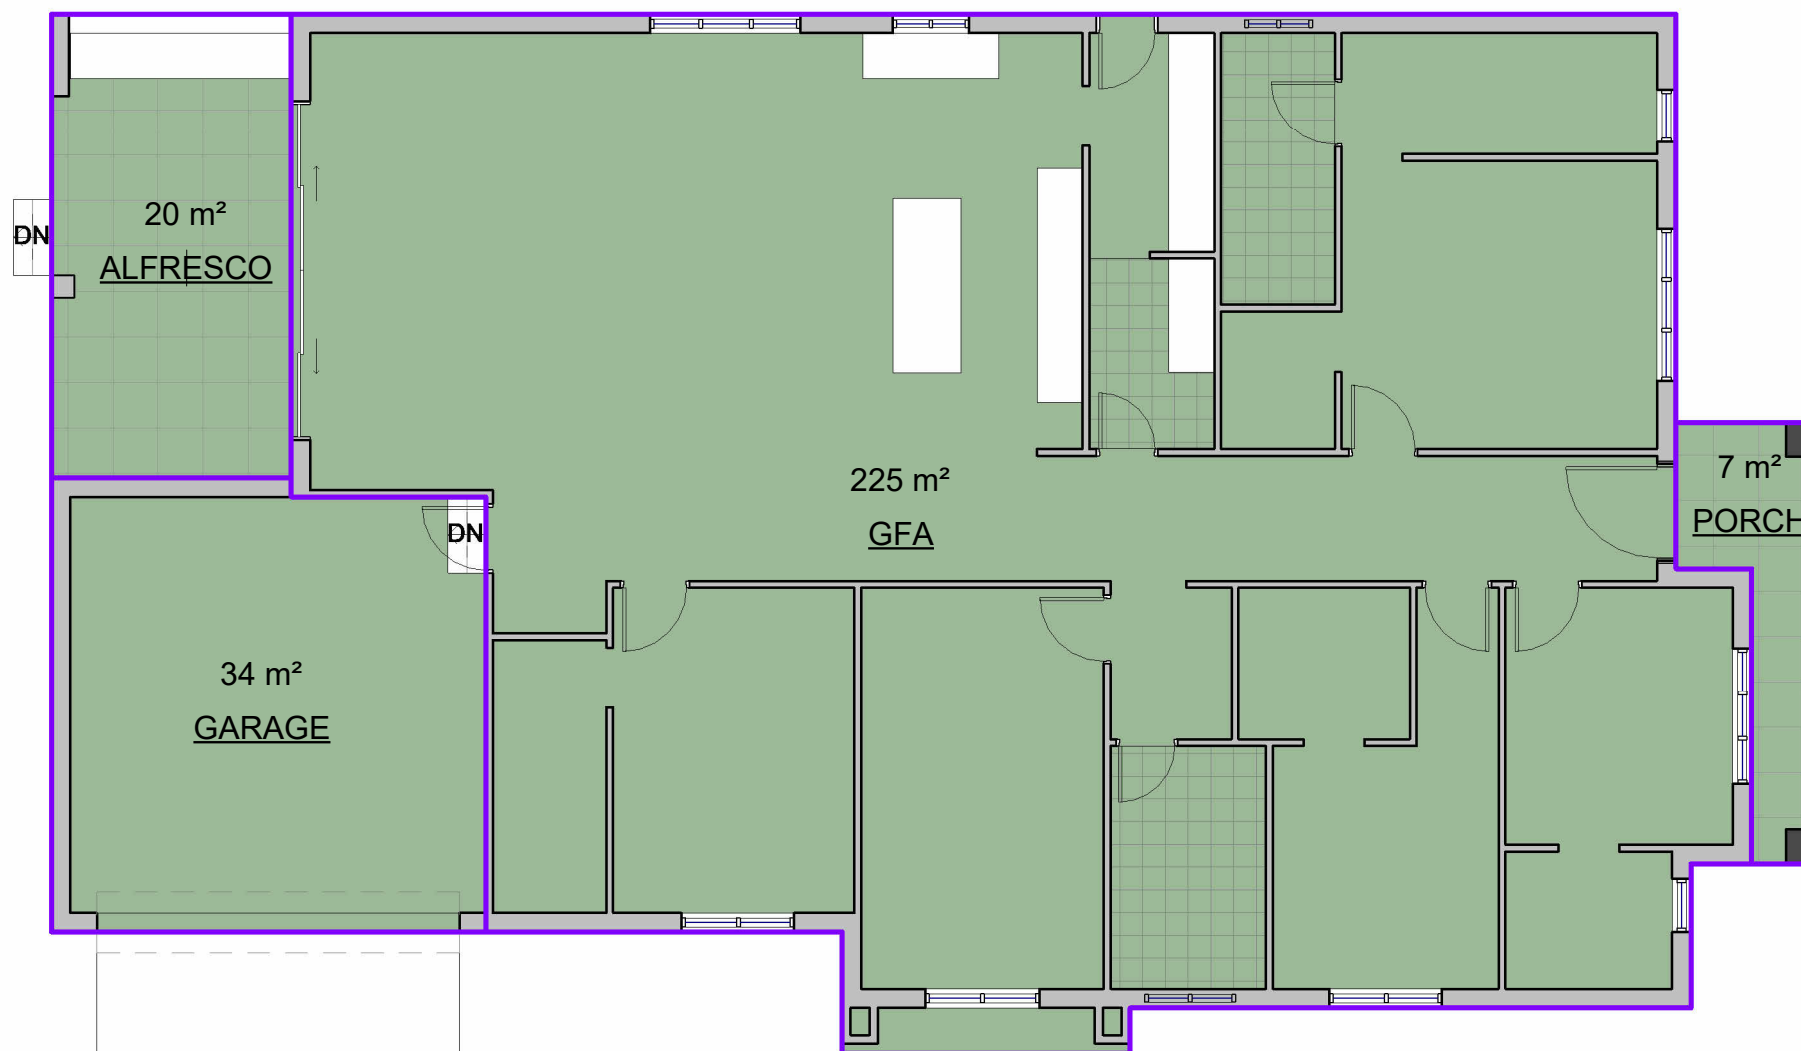

1 Ground Floor
1 : 100


Area Schedule (Gross Building)	
Name	Area


Ground Floor	
GFA	225 m²
GARAGE	34 m²
PORCH	7 m²
ALFRESCO	20 m²
Ground Floor: 4	286 m²
Grand total: 4	286 m²

				CDC ISSUE			
				LOT NO: 2322	DATE: 24-09-2026	SCALE: 1 : 100	DRAWING No: CDC.11
				DRAWN BY: AS	CHECKED BY: RH		REV: 2 ISSUED BY:
				DRAFTED BY: SL	CLIENT NAME: Owner		
2	7-08-2026	CDC ISSUE		PROJECT: LOT 2322 1 HOPPLES ROAD 1 HOPPLES ROAD MENANGLE PARK			
1	10-07-2026	New Concept Plan					
REV	DATE	DESCRIPTION	BY	DRAWING TITLE: FLOOR AREA PLAN			



THIS DRAWING IS THE EXCLUSIVE PROPERTY OF THE DEVELOPER & THE REPRODUCTION OF ANY PART WITHOUT THE PRIOR WRITTEN CONSENT OF THE DEVELOPER IS A VIOLATION OF APPLICABLE LAWS. IN NO EVENT SHALL THE DEVELOPER BE HELD LIABLE FOR SPECIAL COLLATERAL, INCIDENTAL OR CONSEQUENTIAL LIABILITY IN CONNECTION WITH THE USE OF THIS DIGITAL DATA ONCE RELEASED FROM THE DEVELOPER'S OFFICE. THIS DRAWING IS TO BE READ & UNDERSTOOD IN CONJUNCTION WITH THE STRUCTURAL, MECHANICAL, ELECTRICAL & / OR ANY OTHER CONSULTANT'S DOCUMENTATION AS MAY BE APPLICABLE TO THE PROJECT PRIOR TO THE START OF ANY WORKS AND FOR ITS DURATION.

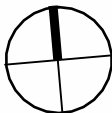

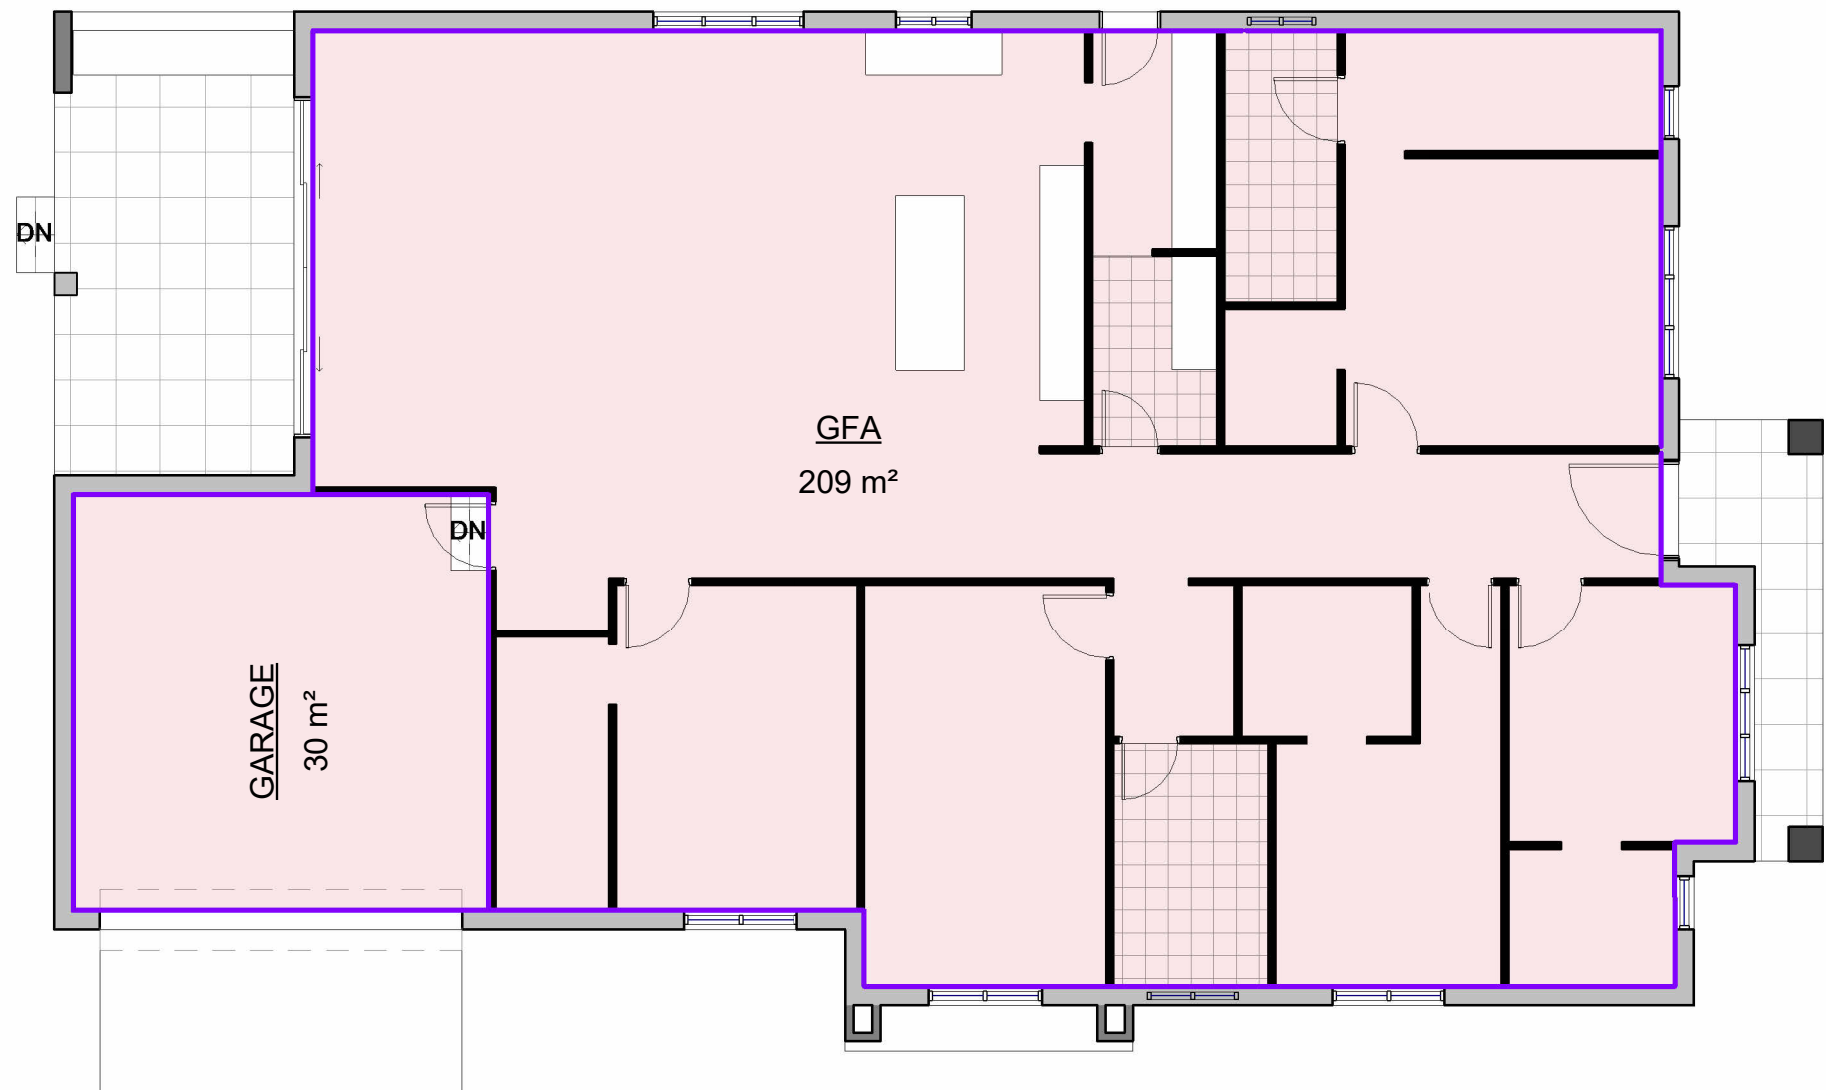

1 Ground Floor
1 : 100

Area Schedule (Rentable)	
Name	Area

Ground Floor	
GFA	209 m²
GARAGE	30 m²
Ground Floor: 2	239 m²
Grand total: 2	239 m²


REV	DATE	DESCRIPTION	BY
2	7-08-2026	CDC ISSUE	



THIS DRAWING IS THE EXCLUSIVE PROPERTY OF THE DEVELOPER & THE REPRODUCTION OF ANY PART WITHOUT THE PRIOR WRITTEN CONSENT OF THE DEVELOPER IS A VIOLATION OF APPLICABLE LAWS. IN NO EVENT SHALL THE DEVELOPER BE HELD LIABLE FOR SPECIAL COLLATERAL, INCIDENTAL OR CONSEQUENTIAL LIABILITY IN CONNECTION WITH THE USE OF THIS DIGITAL DATA ONCE RELEASED FROM THE DEVELOPER'S OFFICE. THIS DRAWING IS TO BE READ & UNDERSTOOD IN CONJUNCTION WITH THE STRUCTURAL, MECHANICAL, ELECTRICAL & / OR ANY OTHER CONSULTANT'S DOCUMENTATION AS MAY BE APPLICABLE TO THE PROJECT PRIOR TO THE START OF ANY WORKS AND FOR ITS DURATION.


PROJECT:
LOT 2322 1 HOPPLES ROAD
1 HOPPLES ROAD MENANGLE PARK





DRAWING TITLE:
RENTABLE AREA PLAN

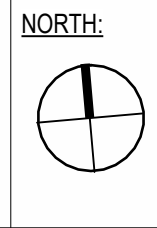

LOT NO: 2322	DATE: 24-09-2026	SCALE: 1 : 100	DRAWING No: CDC.12	REV: 2
DRAWN BY: AS	CHECKED BY: RH	ISSUED BY:		
DRAFTED BY: SL	CLIENT NAME: Owner			


CDC ISSUE

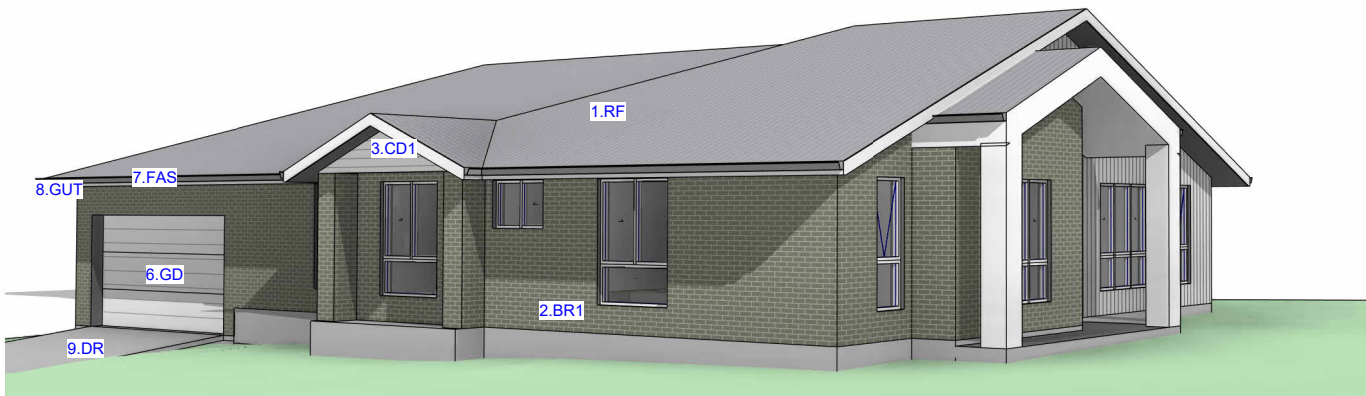

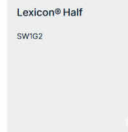   	1. RF	2. BR1	3. CD1	4. AL	5. ED	6. GD	7. FAS	8. GUT	9.DR
	ROOF	MAIN WALLS	CLADDING	WINDOWS/ BALUSTRADE	MAIN DOOR	GARAGE DOOR	FASCIA	GUTTER	DRIVEWAY
MATERIAL	COLORBOND	BRICK	WEATHERBOARD	ALUMINIUM	TIMBER	COLORBOND	COLORBOND	COLORBOND	CONCRETE
COLOUR									
	SOUTHERLY (<0.5 SA)	SILVER BIRCH	LEXICON HALF	WHITE	CHALK U.S.A.	DOVER WHITE	SHALE GREY	SHALE GREY	CHARCOAL

NOTE: ALL COLOURS SPECIFIED ARE INDICATIVE ONLY AND ARE SUBJECT TO VARIATION AND TO AVAILABILITY
ANY DISCREPANCY PLEASE FOLLOW AS PER RENDERED IMAGE

				CDC ISSUE								
				 THIS DRAWING IS THE EXCLUSIVE PROPERTY OF THE DEVELOPER & THE REPRODUCTION OF ANY PART WITHOUT THE PRIOR WRITTEN CONSENT OF THE DEVELOPER IS A VIOLATION OF APPLICABLE LAWS. IN NO EVENT SHALL THE DEVELOPER BE HELD LIABLE FOR SPECIAL COLLATERAL, INCIDENTAL OR CONSEQUENTIAL LIABILITY IN CONNECTION WITH THE USE OF THIS DIGITAL DATA ONCE RELEASED FROM THE DEVELOPER'S OFFICE. THIS DRAWING IS TO BE READ & UNDERSTOOD IN CONJUNCTION WITH THE STRUCTURAL, MECHANICAL, ELECTRICAL & / OR ANY OTHER CONSULTANT'S DOCUMENTATION AS MAY BE APPLICABLE TO THE PROJECT PRIOR TO THE START OF ANY WORKS AND FOR ITS DURATION.	PROJECT: LOT 2322 1 HOPPLES ROAD 1 HOPPLES ROAD MENANGLE PARK	DRAWING TITLE: COLOR SCHEDULE	NORTH:	LOT NO: 2322	DATE: 24-09-2026	SCALE: 1 : 100	DRAWING No: CDC.14	REV: 2
	DRAWN BY: AS	CHECKED BY: RH	ISSUED BY:									
	DRAFTED BY: SL	CLIENT NAME: Owner										
2	7-08-2026	CDC ISSUE										
REV	DATE	DESCRIPTION	BY									

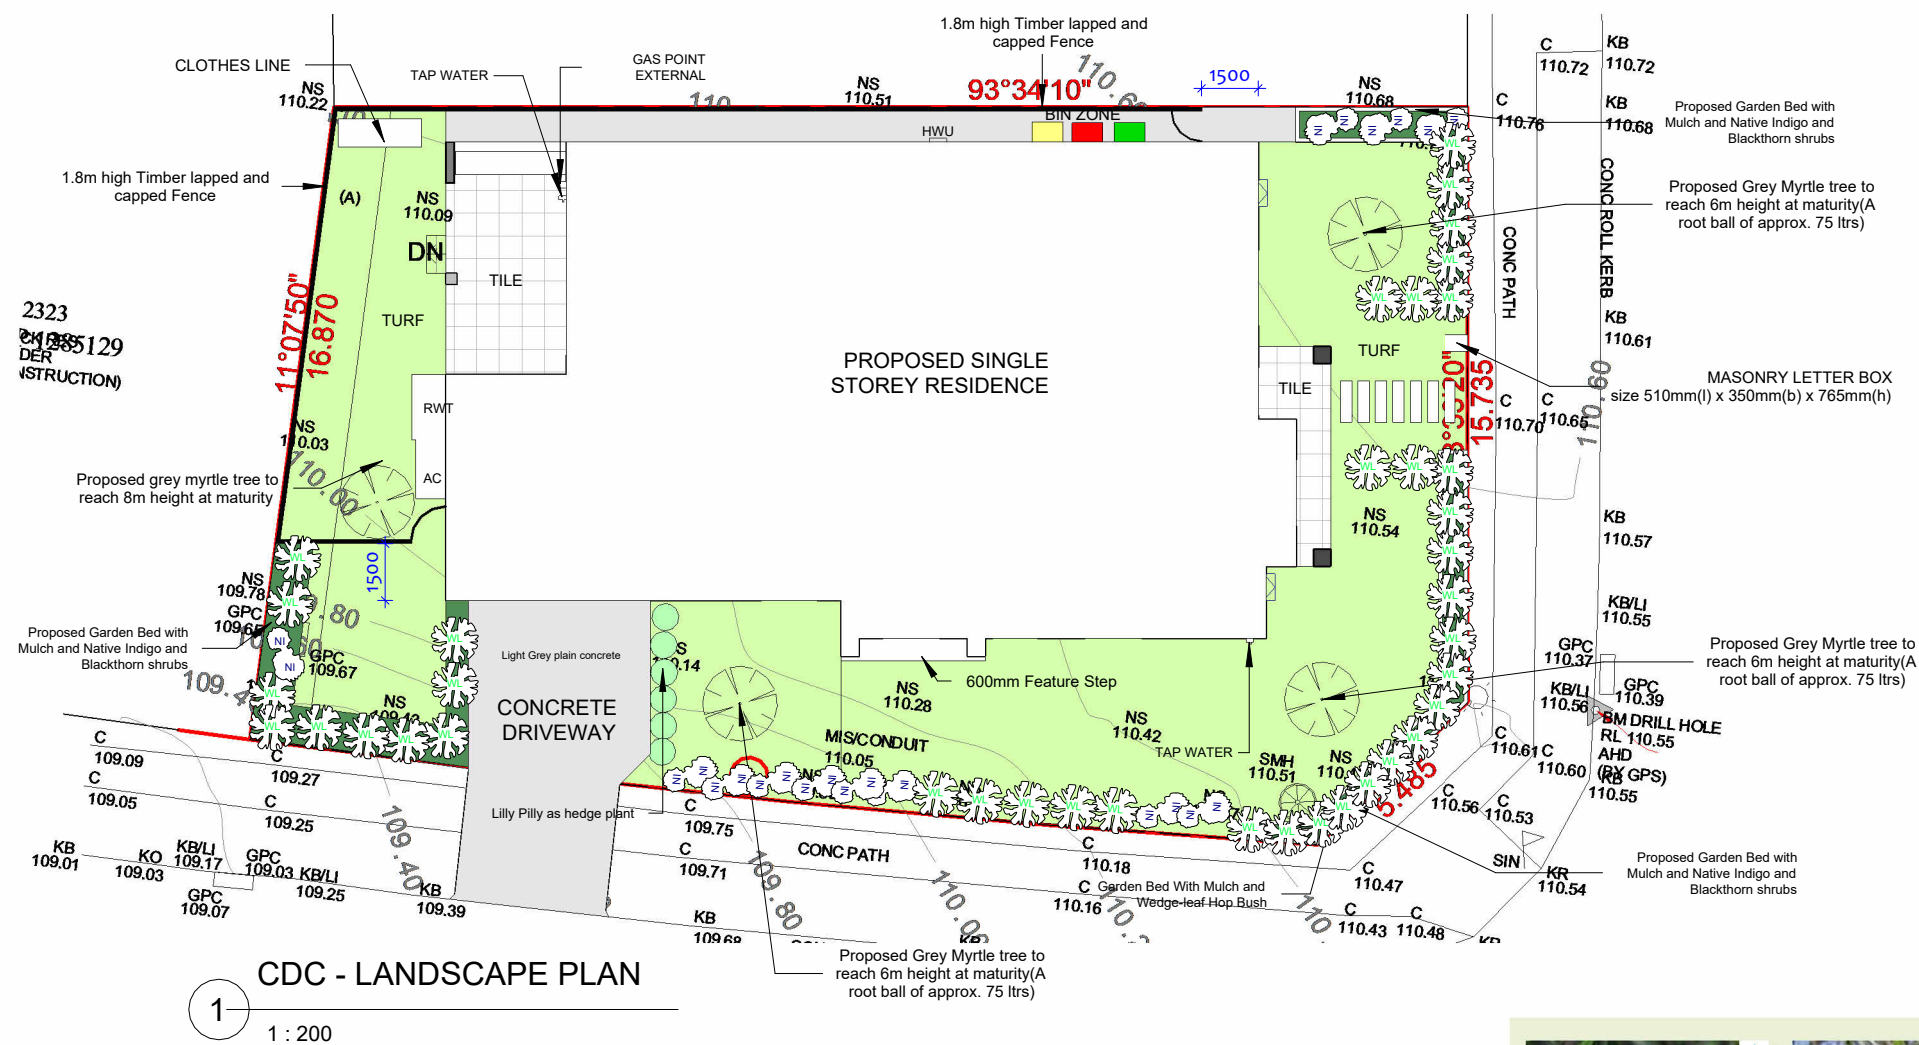

- GENERAL NOTES:**
- LANDSCAPE CONTRACTOR TO CHECK DA CONDITIONS AND STAMPED LANDSCAPE PLAN BEFORE COMMENCING WORKS TO ENSURE NO ADDITIONS/AMENDMENTS TO PLAN.
 - GARDEN BEDS IN OSD BASIN TO CONSIST OF NON FLOATABLE DECORATIVE GRAVEL.
 - REFER TO HYDRAULICS ENGINEERS PLAN FOR OSD DETAILS/FINAL LEVELS.
 - MULCHED PLANTING BEDS TO BE A MINIMUM DEPTH OF 75mm AS SELECTED.
 - CONTRACTOR'S RESPONSIBILITY TO CHECK AND ADJUST SOIL pH AS REQUIRED.
 - PROVIDE TIMBER EDGE AS A MINIMUM BENEATH FENCING/GATES TO DEFINE TURF AND GARDEN BEDS/PATHWAYS. EDGING TO BE PROVIDED TO ALL AREAS WHERE DIFFERING MATERIALS MEET i.e TURF/GARDEN, TURF/GRAVEL PATH ETC.
 - WEED MAT BENEATH GRAVEL GRAVEL PATHWAYS REQUIRED TO LIMIT MUD TRACKING.
 - PREMIUM ORGANIC GARDEN MIX TO BE USED.
 - ALL PLANTS TO BE HEALTHY AND VIGOROUS.
 - CONTRACTOR TO MAKE GOOD TURF ON NATURE STRIP POST CONSTRUCTION.
 - CONTRACTOR TO MAKE GOOD TURF ON NATURE STRIP POST CONSTRUCTION.
 - DO NOT SCALE ARCHITECTURAL SETOUT FROM LANDSCAPE DRAWING.
 - EXISTING TREE SPREAD APPROXIMATE ONLY. REFER TO TREE REPORT WHEN APPLICABLE.
 - SITE SURVEY PROVIDED BY OTHERS.
 - BUFFALO TURF PREFERRED OVER KIKUYU.

LANDSCAPE BASIX NOTE:
THE APPLICANT MUST PLANT INDIGENEOUS OR LOW WATER USE SPECIES OF VEGETATION THROUGHOUT 15 SQM OF THE SITE.

NOTE :BUILDER RESERVES THE RIGHT NOT TO UNDERTAKE NOR SUPPLY CERTIFICATE FOR OCCUPATION CERTIFICATE.
NOTE : TO AID COMPLIANCE WITH BASIX LEGISLATION, PLANTS (WHERE APPLICABLE) HAVE BEEN SELECTED FROM THE LOCAL CITY COUNCIL/SHIRE PLANT LISTS.
NOTE: LOCATION OF SEWER MAINS/LINES, WATER PIPES, UNDERGROUND ELECTRICITY AND OTHER SERVICES MUST BE OBTAINED PRIOR TO COMMENCEMENT OF ANY WORK ON SITE.

CONTRACTORS NOTE : CALCULATED AREAS DETERMINED BY CAD AND HAVE BEEN ROUNDED UP FOR USE AS A GUIDE ONLY ALLOW STANDARD PERCENTAGE FOR CUTTING AND WASTAGE .CONFIRM DIMENSIONS AND NUMBERS PRIOR TO QUOTING/ORDERING.




ZURICH PARCEL MASONRY LETTERBOX
LIGHT GREY COLOUR
CONTEMPORARY STYLE

LANDSCAPE AREA

FRONT AREA	137.5 m ²
BACKYARD AREA	98.9 m ²
TOTAL AREA	236.4 m ²


PLANT SCHEDULE

APNI	Genus	Common Name	Qty	Pot size	Height	Planting Height
	Trees					
103340	Backhousia myrtifolia	Grey Myrtle	4	75L	6-10m	1.5m
	Shrubs					
11033	Bursaria Spinosa Var Sppinosa	Blackthorn, Boxthorn	8	140mm	1.5m	1m
51447278	Dodonea Visco ssp. Cuneata	Wedge-Leaf Hop Bush(WL)	6	140mm	1m	1m
230294	Indigofera Australis	Native Indigo (NI)	5	140mm	1m	1m
	Hedging & screening Plants					
	Acmena smithii 'Cherry Surprise'	Lilly Pilly Cherry Surprise PBR	10	140mm	3m	

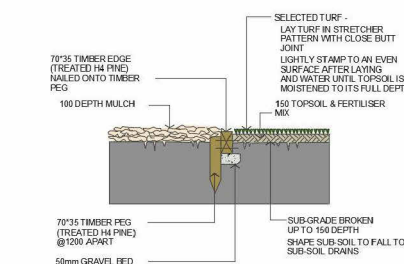

1. TURF & GARDEN EDGE DETAIL

NOTE:
ALIGNMENT OF BRICK EDGE SHALL BE EVEN & FREE FROM DIPS AND HUMPS.

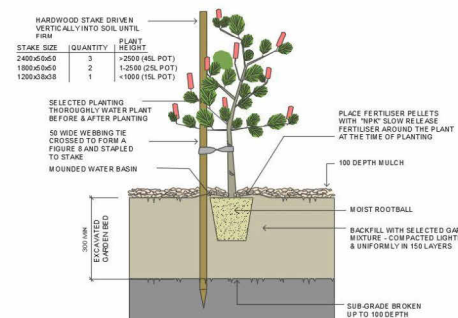

2. TREE & SHRUB PLANTING IN GARDEN BED

NOTE:
DO NOT PLANT IN UNSUITABLE WEATHER CONDITIONS SUCH AS EXTREME HEAT, COLD, WIND OR RAIN.
CLAY SOIL IS TO BE TREATED WITH CLAY BREAKER AND ORGANIC COMPOST.



Bursaria spinosa var spinosa
Blackthorn, Boxthorn
Type: Shrub. Description: Thorny, wiry branches. Leaf size and shape vary's with age. Small, white fragrant flowers. *Height:* Medium. *Flowers:* Jan-April. *Propagation:* sow seed. *Prune:* after flowering, only to maintain shape.



Dodonea viscosa ssp. Cuneata
Wedge-leaf Hop Bush
Type: Shrub. Description: Compact growth. Sticky leaves taper to sharp point. Green fruit turns red and purple. *Height:* 1m. *Flowers:* Spring. *Propagation:* sow from seed or take cutting in Spring and Summer. *Prune:* minimally.



Indigofera australis
Native Indigo
Type: Shrub. Description: Slender, erect. Pink to lilac pea flowers, numerous along stems. *Height:* 1m Alluvial Aug-Sept. *Flowers:* Spring. *Propagation:* from cutting, early to mid Summer. *Prune:* trim lightly after flowering.



Backhousia myrtifolia
Grey Myrtle
Type: Tree. Description: Dense feature tree with, green glossy foliage. Greenish yellow flowers in small terminal clusters. *Height:* 6-10m. *Flowers:* Nov-Dec. *Propagation:* sow seed in Spring. *Prune:* minimally.

CDC ISSUE


REV	DATE	DESCRIPTION	BY
2	7-08-2026	CDC ISSUE	



THIS DRAWING IS THE EXCLUSIVE PROPERTY OF THE DEVELOPER & THE REPRODUCTION OF ANY PART WITHOUT THE PRIOR WRITTEN CONSENT OF THE DEVELOPER IS A VIOLATION OF APPLICABLE LAWS. IN NO EVENT SHALL THE DEVELOPER BE HELD LIABLE FOR SPECIAL COLLATERAL, INCIDENTAL OR CONSEQUENTIAL LIABILITY IN CONNECTION WITH THE USE OF THIS DIGITAL DATA ONCE RELEASED FROM THE DEVELOPER'S OFFICE. THIS DRAWING IS TO BE READ & UNDERSTOOD IN CONJUNCTION WITH THE STRUCTURAL, MECHANICAL, ELECTRICAL & / OR ANY OTHER CONSULTANT'S DOCUMENTATION AS MAY BE APPLICABLE TO THE PROJECT PRIOR TO THE START OF ANY WORKS AND FOR ITS DURATION.

PROJECT:
LOT 2322 1 HOPPLES ROAD
1 HOPPLES ROAD MENANGLE PARK

DRAWING TITLE:
LANDSCAPE PLAN

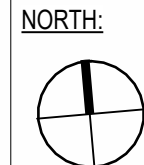

LOT NO:	DATE:	SCALE:	DRAWING No:	REV:
2322	24-09-2026	1 : 200	CDC.15	2
DRAWN BY:	CHECKED BY:	CLIENT NAME:	ISSUED BY:	
AS	RH	Owner		

ABCB HOUSING PROVISIONS : PART 10.2 WET AREA WATERPROOFING

10.2.1 Wet Areas

1. Building elements in wet areas within a building must be protected with a waterproofing system.
2. The waterproofing system in (1) must be either waterproof or water resistant in accordance with 10.2.2 to 10.2.6.

10.2.2 Shower Area (enclosed and unenclosed)

1. For a shower area with a hob, step-down or level threshold, the following applies:
- a. The floor of the *shower area* must be *waterproof*, including any hob or step-down (see Figure 10.2.2); and
- b. The walls of the *shower area* must be *waterproof* not less than 1800 mm above the floor substrate (see Figure 10.2.2).
- c. Wall junctions and joints within the *shower area* must be *waterproof* not less than 40 mm either side of the junction (see Figure 10.2.2).
- d. Wall/floor junctions within the shower area must be *waterproof* (see Figure 10.2.2).
- e. Penetrations within the *shower area* must be *waterproof*.
2. A shower with a *preformed shower base* must also comply with the requirements of (1), except for (a) which is not applicable.

Figure 10.2.2: Extent of treatment for shower areas - concrete compressed fibre-cement and fibre-cement sheet floors.

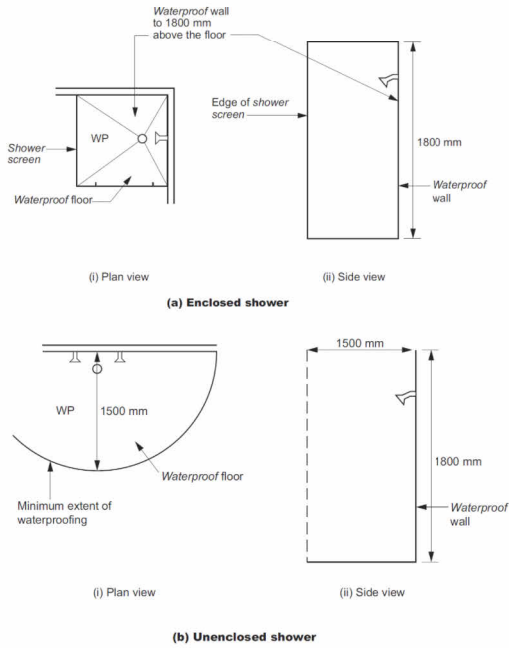


Figure Notes
Wall/floor junction heights are to be as per 10.2.2 to 10.2.6 (as applicable).

Notes
Where a shower is above a bath or spa, use requirements for shower.

10.2.3 Area outside shower area

1. For concrete, compressed fibre-cement and fibre-cement sheet flooring, the floor of the room must be water resistant.
2. For timber floors including particleboard, plywood and other timber based flooring materials, the floor of the room must be *waterproof*.
3. Wall/floor junctions must be -
- a. *waterproof*, and
- b. where a flashing is used, the horizontal leg must be not less than 40 mm.

10.2.4 Areas adjacent to baths and spas without showers

1. For areas adjacent to all baths and spas, the following applies:
- a. For concrete, compressed fibre-cement and fibre-cement sheet flooring, the floor of the room must be water resistant.
- b. For timber floors including particleboard, plywood and other timber based flooring materials, the floor of the room must be *waterproof*.
- c. Tap and spout penetrations must be waterproof where they occur in horizontal surfaces.
2. For areas adjacent to non-freestanding baths and spas, the following applies:
- a. Walls must be water resistant (see Figure 10.2.4a and Figure 10.2.4b)-
- to a height of not less than 150mm above the vessel, for the extent of the vessel, where the vessel is within 75mm of a wall; and
 - for all exposed surfaces below vessel lip.
- b. Wall junctions and joints must be water resistant within 150mm above a vessel for the extent of the vessel.
- c. Wall/floor junctions must be *waterproof* for the extent of the vessel (see Figure 10.2.4a and Figure 10.2.4b).
3. For inserted baths and spas, the following applies:
- a. For floors and horizontal surfaces:
- Any shelf area adjoining the bath or spa must be waterproof and include a waterstop under the vessel lip.
 - There are no requirements for the floor under a bath or spa.
- b. For walls:
- Waterproof to not less than 150mm above the lip of a bath or spa.
 - There are no requirements for the floor under a bath or spa.
- c. For wall junctions and joints, the following applies:
- Waterproof junctions within 150mm of a bath or spa.
 - There are no requirements for junctions and joints in walls beneath the lip of a bath or spa.
- d. Tap and spout penetrations must be waterproof where they occur in horizontal surfaces.

Figure 10.2.4a: Areas adjacent to baths and spas without showers for concrete, compressed fibre-cement and fibre-cement sheet flooring




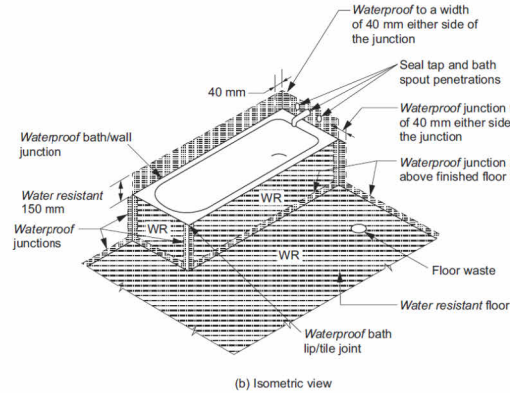



Figure 10.2.4b: Areas adjacent to baths and spas without showers for timber floors including particle-board, plywood and other floor materials

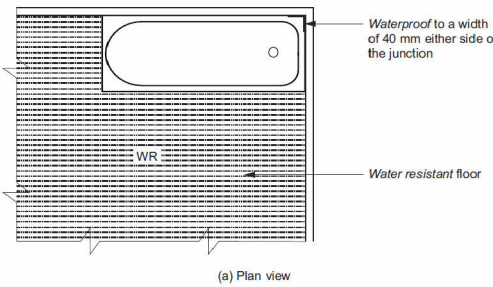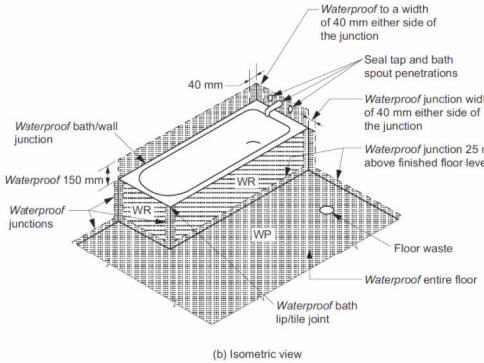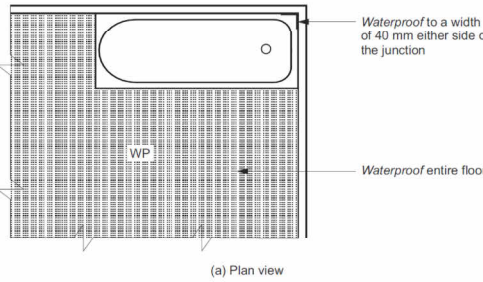

10.2.5 Other areas

1. For walls adjoining other types of vessels (e.g. sink, basin or laundry tub), the following applies:
- a. Walls must be water resistant to a height of not less than 150mm above the vessel, for the extent of the vessel, where the vessel is within 75 mm of a wall (see Figure 10.2.5.)
- b. Waterproof wall junctions where a vessel is fixed to a wall.
- c. Waterproof tap and spout penetrations where they occur in surfaces required to be waterproof or water resistant.
2. For laundries and WCs, the following applies:
- a. The floor of the room must be water resistant.
- b. Wall/floor junctions must be water resistant, and where a flashing is used, the horizontal leg must not be less than 40 mm.
3. For WCs with handheld bidet spray installations, the following applies:
- a. The floor of the room must be waterproof.
- b. Walls must be -
- waterproof in WC area within a 900 mm radius from the wall connection of the handheld bidet spray device to a height of not less than 150mm above the floor substrate; and
 - water resistant in WC area within a 900 mm radius from the wall connection of the handheld bidet device to not less than 1200 mm above the finished floor level of the WC.
- c. Wall junctions within the WC area within 900 mm radius from the wall connection of the handheld bidet spray device must be waterproof.
- d. Wall/floor junctions within the WC area within 1000 mm radius from the wall connection of the handheld bidet spray device must be waterproof.
- e. Penetrations in the WC area must be waterproof.

Figure 10.2.5: Bath and vessel abutting wall - areas to be protected

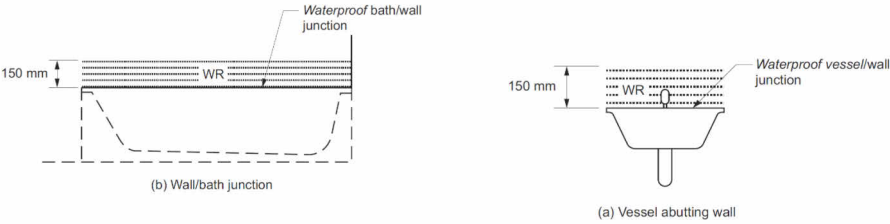

10.2.6 Waterproofing systems

1. For the purposes of this Part, a waterproofing system is deemed -
- a. *waterproof*, if it complies with (2); or
- b. *water resistant*, if it complies with (3).
2. For a waterproofing system required to be *waterproof* in accordance with 10.2.2 to 10.2.5, the materials nominated in 10.2.8 must be used.
3. For a waterproofing system required to be *water resistant* in accordance with 10.2.2 to 10.2.5, the materials nominated in 10.2.9 must be used in conjunction with the materials in 10.2.10.

10.2.12 Construction of wet area floors - falls

- Where a floor waste is installed -
- a. the minimum continuous fall of a floor plane to the waste must be 1:80; and
- b. the maximum continuous fall of a floor plane to the waste must be 1:50.

				CDC ISSUE			
				LOT NO: 2322	DATE: 24-09-2026	SCALE: 1 : 50	DRAWING No: REV: 2
				DRAWN BY: AS	CHECKED BY: RH		ISSUED BY:
				DRAFTED BY: SL	CLIENT NAME: Owner		
2	7-08-2026	CDC ISSUE					
REV	DATE	DESCRIPTION	BY				

THIS DRAWING IS THE EXCLUSIVE PROPERTY OF THE DEVELOPER & THE REPRODUCTION OF ANY PART WITHOUT THE PRIOR WRITTEN CONSENT OF THE DEVELOPER IS A VIOLATION OF APPLICABLE LAWS. IN NO EVENT SHALL THE DEVELOPER BE HELD LIABLE FOR SPECIAL COLLATERAL, INCIDENTAL OR CONSEQUENTIAL LIABILITY IN CONNECTION WITH THE USE OF THIS DIGITAL DATA ONCE RELEASED FROM THE DEVELOPER'S OFFICE. THIS DRAWING IS TO BE READ & UNDERSTOOD IN CONJUNCTION WITH THE STRUCTURAL, MECHANICAL, ELECTRICAL & / OR ANY OTHER CONSULTANT'S DOCUMENTATION AS MAY BE APPLICABLE TO THE PROJECT PRIOR TO THE START OF ANY WORKS AND FOR ITS DURATION.

PROJECT:
LOT 2322 1 HOPPLES ROAD
1 HOPPLES ROAD MENANGLE PARK

DRAWING TITLE:
WATERPROOFING DETAILS

NORTH:

LOT NO:
2322

DATE:
24-09-2026

SCALE:
1 : 50

DRAWING No:
REV: 2

DRAFTED BY:
SL

CLIENT NAME:
Owner