

FOR CONSTRUCTION

LOT 114 47 TWELFTH AVENUE AUSTRAL

PROPOSED CONSTRUCTION OF A TWO STOREY DWELLING



OnBuild Certifiers Pty Ltd
Reference: 260016
Date: 15/04/2026
Andrew Soliman
Director/ Principal Certifier
BDC2940
Consultant who prepared this document remains responsible for accuracy

BASIX COMMITMENTS		Certificate number: 08410055 Date of issue: Wednesday, 08 April 2026
WATER		
LANDSCAPE	74m2	
TOILETS	4 STARS	
KITCHEN TAPS	4 STARS	
SHOWER HEADS	4 STAR (>4.5 but <=6 Umin)	
BASIN TAPS	4 STARS	
ALTERNATIVE WATER	1500L RAINWATER TANK	
ROOF WATER TO TANK	200m2	
ALT.WATER USES- TANK	LAUNDRY	
ALT. WATER USES - RETIC	ALL TOILETS + ONE OUTDOOR TAP	
SWIMMING POOL	N/A	
ENERGY		
HOT WATER	GAS INSTANTANEOUS - 5 STAR	
AIR-CON (HEATING)	3 PHASE DUCTED - EER 3.0-3.5	
AIR-CON (COOLING)	3 PHASE DUCTED - EER 3.0-3.5	
VENTILATION - BATHROOM	NONE/ NATURAL VENTILATION	
VENTILATION - KITCHEN	DUCTED - MANUAL SWITCH	
VENTILATION - LAUNDRY	NONE/ NATURAL VENTILATION	
PV SYSTEM	N/A	
COOKTOP	GAS	
OVEN	ELECTRIC	
CLOTHES DRYING	OUTDOOR CLOTHESLINE	
LIGHTING	DEDICATED LED	

AC	AIR CONDITIONING UNIT
AL	POWDERCOATED ALUMINIUM DOOR/ WINDOW
BS	BALUSTRADE TYPE
BG	BOX GUTTER
BR	BRICK FACED
CAP	METAL CAPPING
CD1, CD2, etc.	WALL CLADDING
CONC.	CONCRETE FLOOR
CPT	CARPET
CRT	CONCRETE ROOF TILES
CR1, CR2, etc.	CEMENT RENDER TYPE/ COLOUR
DP/S	DOWN PIPE
DW	DISH WASHER
ED	ENTRY DOOR
F	FRIDGE
FAS	FASCIA
FET	FEATURE TILE
FT, FT1, FT2, etc.	FLOOR TILES
FW	FLOOR WASTE
GD	GARAGE DOOR
GUT	GUTTER
HWU	HOT WATER UNIT
HYB	HYBRID FLOOR
L	LINEN
MR	METAL ROOF
MW	MICROWAVE OVEN
NGL	NATURAL GROUND LEVEL
OBS	OBSCURSED GLASS
P	PANTRY
R	ROBE
RL	REDUCED LEVEL
RWH	RAIN WATER HEAD
RWT	RAIN WATER TANK
S	STORAGE
TOW	TOP OF WALL
TL	TIMBER LAMINATE
WC	WATER CLOSET
WM	WASHING MACHINE
SD	SMOKE DETECTOR

Sheet List				
Sheet Number	Sheet Name	Drawn By	Current Revision Date	Revision
CDC.01	COVER SHEET	AS	3-02-2026	CDC ISSUE
CDC.02	GENERAL NOTES	AS	3-02-2026	CDC ISSUE
CDC.02B	GENERAL NOTES B	AS	3-02-2026	CDC ISSUE
CDC.03	LOCATION PLAN AND SITE PLAN	AS	3-02-2026	CDC ISSUE
CDC.04	SITE ANALYSIS AND SEDIMENT CONTROL PLAN	AS	3-02-2026	CDC ISSUE
CDC.05	GROUND FLOOR PLAN	AS	3-02-2026	CDC ISSUE
CDC.06	FIRST FLOOR PLAN	AS	3-02-2026	CDC ISSUE
CDC.07	ROOF PLAN	AS	3-02-2026	CDC ISSUE

Sheet List				
Sheet Number	Sheet Name	Drawn By	Current Revision Date	Revision
CDC.08	ELEVATIONS 01	AS	3-02-2026	CDC ISSUE
CDC.09	ELEVATIONS 02	AS	3-02-2026	CDC ISSUE
CDC.10	SECTIONS	AS	3-02-2026	CDC ISSUE
CDC.11	GROSS FLOOR AREA PLAN	AS	3-02-2026	CDC ISSUE
CDC.12	RENTABLE FLOOR AREA PLAN	AS	3-02-2026	CDC ISSUE
CDC.14	COLOR SCHEDULE	AS	3-02-2026	CDC ISSUE
CDC.15	LANDSCAPE PLAN	AS	3-02-2026	CDC ISSUE
CDC.18	WATERPROOFING DETAILS	AS	3-02-2026	CDC ISSUE

NOTE: ALL IMAGES ARE FOR ILLUSTRATION ONLY AND ARE SUBJECT TO VARIATION AND TO AVAILABILITY OF MATERIALS.

REV	DATE	DESCRIPTION	BY
3	3-02-2026	CDC ISSUE	
1	9-12-2025	Living & Alfresco extended to increase 5 sqm by Nava	

THIS DRAWING IS THE EXCLUSIVE PROPERTY OF THE DEVELOPER & THE REPRODUCTION OF ANY PART WITHOUT THE PRIOR WRITTEN CONSENT OF THE DEVELOPER IS A VIOLATION OF APPLICABLE LAWS. IN NO EVENT SHALL THE DEVELOPER BE HELD LIABLE FOR SPECIAL, COLLATERAL, INCIDENTAL OR CONSEQUENTIAL LIABILITY IN CONNECTION WITH THE USE OF THIS DIGITAL DATA ONCE RELEASED FROM THE DEVELOPER'S OFFICE. THIS DRAWING IS TO BE READ & UNDERSTOOD IN CONJUNCTION WITH THE STRUCTURAL, MECHANICAL, ELECTRICAL & / OR ANY OTHER CONSULTANT'S DOCUMENTATION AS MAY BE APPLICABLE TO THE PROJECT PRIOR TO THE START OF ANY WORKS AND FOR ITS DURATION.

PROJECT:
LOT 114 47 TWELFTH AVENUE
47 TWELFTH AVENUE
AUSTRAL

DRAWING TITLE:
COVER SHEET



LOT NO:	DATE:	SCALE:	DRAWING No:	REV:
114	15-04-2026	As indicated	CDC.01	3
DRAWN BY:	CHECKED BY:			ISSUED BY:
AS	RH			
DRAFTED BY:	CLIENT NAME:			
SL	Abi Maharjan & Nikki Manandhar			

BUILDING SPECIFICATIONS

National Construction Code – Volume 2, Amendment 1 – Building Code of Australia 2022 & Housing Provisions Standard 2022

SITE PREPARATION

- PART 3.1 OF THE NCC VOLUME 2, AMENDMENT 1 - BUILDING CODE OF AUSTRALIA 2022 & HOUSING PROVISIONS STANDARD 2022.

EARTHWORKS

- TO BE CARRIED OUT IN ACCORDANCE WITH THE REQUIREMENTS OF THE ENVIRONMENTAL PLANNING & ASSESSMENT ACT 1979 AND DEVELOPMENT CONSENT CONDITIONS
- PART 3.2 OF THE NCC VOLUME 2, AMENDMENT 1 - BUILDING CODE OF AUSTRALIA 2022 & HOUSING PROVISIONS STANDARD 2022.
- AS 4678:2002 - EARTH-RETAINING STRUCTURES

DRAINAGE

- PART 3.3 OF THE NCC VOLUME 2, AMENDMENT 1 - BUILDING CODE OF AUSTRALIA 2022 & HOUSING PROVISIONS STANDARD 2022.
- AS/NZS 3500.1:2021 - PLUMBING & DRAINAGE - WATER SERVICES
- AS/NZS 3500.2:2021 - PLUMBING & DRAINAGE - SANITARY PLUMBING & DRAINAGE
- AS/NZS 3500.3:2021 - PLUMBING & DRAINAGE STORMWATER DRAINAGE
- AS/NZS 3500.4:2021 - PLUMBING & DRAINAGE - HEATED WATER SERVICES

STRUCTURAL WORK

- Part 2.2 OF THE NCC VOLUME 2, AMENDMENT 1 - BUILDING CODE OF AUSTRALIA 2022 & HOUSING PROVISIONS STANDARD 2022.
- AS 4100:2020 - STEEL STRUCTURES CODES
- AS/NZS 1170.0:2002 - GENERAL PRINCIPLES
- AS/NZS 1170.1:2002 - PARTS 1 PERMANENT, IMPOSED AND OTHER ACTIONS
- AS/NZS 1170.2:2021 - PART 2 WIND ACTIONS
- AS 3700:2018 - SAA MASONRY CODE
- AS 1684.3:2021 - RESIDENTIAL TIMBER FRAMED CONSTRUCTION

FOOTINGS & SLABS

- PART 4 OF THE NCC VOLUME 2, AMENDMENT 1 - BUILDING CODE OF AUSTRALIA 2022 & HOUSING PROVISIONS STANDARD 2022.
- AS 2159:2009 - PILING - DESIGN & INSTALLATION
- AS 2870:2011 - RESIDENTIAL SLABS & FOOTINGS
- AS 3600:2018 - CONCRETE STRUCTURES

MASONRY

- PART 5 OF THE NCC VOLUME 2, AMENDMENT 1 - BUILDING CODE OF AUSTRALIA 2022 & HOUSING PROVISIONS STANDARD 2022.
- AS 3700:2018 - MASONRY STRUCTURES

FRAMING

- PART 6 OF THE NCC VOLUME 2, AMENDMENT 1 - BUILDING CODE OF AUSTRALIA 2022 & HOUSING PROVISIONS STANDARD 2022.
- AS 1684.2:2021 - RESIDENTIAL TIMBER-FRAMED CONSTRUCTION - NON- CYCLONIC AREAS
- AS 1720.1:2010 - TIMBER STRUCTURES - DESIGN METHODS
- AS 4100:2020 - STEEL STRUCTURES
- AS 3660.1:2014 - TERMITE MANAGEMENT SYSTEM

ROOF & WALL CLADDING

- PART 7 OF THE NCC VOLUME 2, AMENDMENT 1 - BUILDING CODE OF AUSTRALIA 2022 & HOUSING PROVISIONS STANDARD 2022.
- AS 1273:1991 - UNPLASTICIZED PVC (UPVC) DOWNPIPES & FITTINGS FOR RAINWATER
- AS 1562.1:2018 - DESIGN & INSTALLATION OF SHEET ROOF & WALL CLADDING - METAL
- AS/NZS 1562.3:2006 - DESIGN & INSTALLATION OF SHEET ROOF & WALL CLADDING - PLASTIC
- AS 2049:2002 - ROOF TILES
- AS 2050:2018 - INSTALLATION OF ROOF TILES
- AS 4285:2019 - ROOFLIGHTS

GLAZING

- PART 8 OF THE NCC VOLUME 2, AMENDMENT 1 - BUILDING CODE OF AUSTRALIA 2022 & HOUSING PROVISIONS STANDARD 2022.
- AS 1288:2021 - GLASS IN BUILDINGS - SELECTION & INSTALLATION
- AS 2047:2014 - WINDOWS & EXTERNAL GLAZED DOORS IN BUILDINGS
- AS/NZS 2208:1996 - SAFETY GLAZING MATERIALS IN BUILDINGS

FIRE SAFETY

- PART 9 OF THE NCC VOLUME 2, AMENDMENT 1 - BUILDING CODE OF AUSTRALIA 2022 & HOUSING PROVISIONS STANDARD 2022.
- AS 3786:2014 - SMOKE ALARMS USING SCATTERED LIGHT, TRANSMITTED LIGHT OR IONIZATION

HEALTH & AMENITY

- PART 10 OF THE NCC VOLUME 2, AMENDMENT 1 - BUILDING CODE OF AUSTRALIA 2022 & HOUSING PROVISIONS STANDARD 2022.
- AS/NZS ISO 717.1:2004 - ACOUSTICS - RATING OF SOUND INSULATION IN BUILDINGS & OF BUILDING ELEMENTS - AIRBORNE SOUND INSULATION
- AS ISO 717.2:2004 - ACOUSTICS - RATING OF SOUND INSULATION IN BUILDINGS & OF BUILDING ELEMENTS - IMPACT SOUND INSULATION
- AS 1668.2:2012 - THE USE OF VENTILATION & AIR CONDITIONING IN BUILDINGS - MECHANICAL VENTILATION IN BUILDINGS
- AS 1668.4:2012 - THE USE OF VENTILATION & AIR CONDITIONING IN BUILDINGS - NATURAL VENTILATION OF BUILDINGS
- AS/NZS 1680.0:2009 - INTERIOR LIGHTING - SAFE MOVEMENT
- AS 3740:2021 - WATERPROOFING OF DOMESTIC WET AREAS
- AS 3000:2018 - ELECTRICAL INSTALLATION
- BCA Part 10.8.1, AS4200.1 & AS4200.2 - PLIABLE BUILDING MEMBRANE INSTALLED.

WATERPROOFING

- PART 10.2 OF THE NCC VOLUME 2, AMENDMENT 1 - BUILDING CODE OF AUSTRALIA 2022 & HOUSING PROVISIONS STANDARD 2022
- AS 3740:2021 - WATERPROOFING TO WET AREA
- AS 4654:2012 - EXTERNAL WET AREAS

SAFE MOVEMENT & ACCESS

- PART 11 OF THE NCC VOLUME 2, AMENDMENT 1 - BUILDING CODE OF AUSTRALIA 2022 & HOUSING PROVISIONS STANDARD 2022.
- AS 1428.1:2009 - DESIGN FOR ACCESS & MOBILITY - GENERAL REQUIREMENTS FOR ACCESS - NEW BUILDING WORK
- AS 1657:2018 - FIXED PLATFORMS, WALKWAYS, STAIRWAYS & LADDERS - DESIGN, CONSTRUCTION & INSTALLATION

OnBuild Certifiers Pty Ltd
HANDRAILS & BALUSTRADE
Reference: 260016
PART 11.3.3 OF THE NCC VOLUME 2, AMENDMENT 1 - BUILDING CODE OF AUSTRALIA 2022 & HOUSING PROVISIONS STANDARD 2022.
PART 11.3.4 OF THE NCC VOLUME 2, AMENDMENT 1 - BUILDING CODE OF AUSTRALIA 2022 & HOUSING PROVISIONS STANDARD 2022.
PART 11.3.5 OF THE NCC VOLUME 2, AMENDMENT 1 - BUILDING CODE OF AUSTRALIA 2022 & HOUSING PROVISIONS STANDARD 2022.
AS 1170.1:2002 - BALUSTRADE INSTALLATION
PROTECTION OF OPENABLE WINDOW
PART 11.3.7 AND 11.3.8 OF THE NCC VOLUME 2, AMENDMENT 1 - BUILDING CODE OF AUSTRALIA 2022 & HOUSING PROVISIONS STANDARD 2022.

Consultant responsible for accuracy
Tentative

ENERGY EFFICIENCY
PART 13 OF THE NCC VOLUME 2, AMENDMENT 1 - BUILDING CODE OF AUSTRALIA 2022 & HOUSING PROVISIONS STANDARD 2022 & BASIX CERTIFICATE.

MECHANICAL VENTILATION
- EXHAUST FROM A BATHROOM, SANITARY COMPARTMENT TO DISCHARGE DIRECTLY TO OUTDOOR AIR WITH MINIMUM FLOW RATE OF 25L/S & MAKE-UP AIR VIA OPENINGS TO AN ADJACENT ROOM WITH A FREE AREA OF 14,000 MM². THIS EXHAUST SYSTEM MUST BE INTERLOCKED WITH LIGHT SWITCH AND INCLUDE RUN-ON TIMER SO THAT THE EXHAUST SYSTEM CONTINUES TO OPERATE FOR 10 MINUTES AFTER THE LIGHT SWITCH IS OFF.

- ANY INSTALLED - KITCHEN RANGEHOOD EXHAUST TO DISCHARGE DIRECTLY OR VIA DUCT TO OUTDOOR AIR WITH MINIMUM FLOW RATE OF 40L/S & MAKE-UP AIR VIA OPENINGS TO AN ADJACENT ROOM WITH A FREE AREA OF 14,000 MM².

- LAUNDRY EXHAUST TO DISCHARGE DIRECTLY OR VIA DUCT TO OUTDOOR AIR WITH MINIMUM FLOW RATE OF 40L/S & MAKE-UP AIR VIA OPENINGS TO AN ADJACENT ROOM WITH A FREE AREA OF 14,000 MM².



REV	DATE	DESCRIPTION	BY
3	3-02-2026	CDC ISSUE	
1	9-12-2025	Living & Alfresco extended to increase 5 sqm by Nava	



THIS DRAWING IS THE EXCLUSIVE PROPERTY OF THE DEVELOPER & THE REPRODUCTION OF ANY PART WITHOUT THE PRIOR WRITTEN CONSENT OF THE DEVELOPER IS A VIOLATION OF APPLICABLE LAWS. IN NO EVENT SHALL THE DEVELOPER BE HELD LIABLE FOR SPECIAL, COLLATERAL, INCIDENTAL OR CONSEQUENTIAL LIABILITY IN CONNECTION WITH THE USE OF THIS DIGITAL DATA ONCE RELEASED FROM THE DEVELOPER'S OFFICE. THIS DRAWING IS TO BE READ & UNDERSTOOD IN CONJUNCTION WITH THE STRUCTURAL, MECHANICAL, ELECTRICAL & / OR ANY OTHER CONSULTANT'S DOCUMENTATION AS MAY BE APPLICABLE TO THE PROJECT PRIOR TO THE START OF ANY WORKS AND FOR ITS DURATION.

PROJECT:
**LOT 114 47 TWELFTH
AVENUE
47 TWELFTH AVENUE
AUSTRAL**

DRAWING TITLE:
GENERAL NOTES

NORTH:

LOT NO:	DATE:	SCALE:	DRAWING No:	REV:
114	15-04-2026	1 : 2	CDC.02	3
DRAWN BY:	CHECKED BY:	CLIENT NAME:	ISSUED BY:	
AS	RH	Abi Maharjan & Nikki Manandhar		
DRAFTED BY:				
SL				

CDC ISSUE

TERMITE SHEET

- TERMITE SHEET EXTENDS THROUGH THE ENTIRE MASONRY LEAF AND IS VISIBLE AT THE FINISHED FACE OF THE WALL.


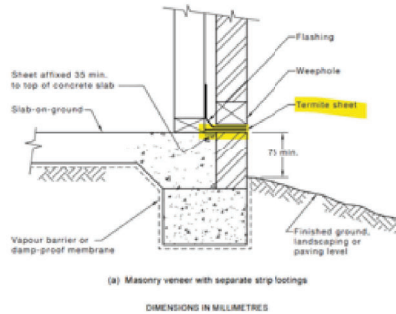


FIGURE 5.5 (in part) TYPICAL SHEET INSTALLATION TO EXTERNAL WALL WITH CONCRETE FLOOR SLAB

DPC FOR BRICKS

DAMP-PROOF COURSE (DPC) TO EXTENDS THROUGH THE ENTIRE MASONRY LEAF AND NEED TO BE VISIBLE AT THE FINISHED FACE OF THE WALL FROM OUTSIDE

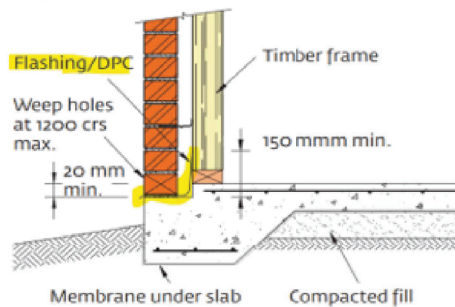

DEMOLITION

- AS 2601-2001 – DEMOLITION WORK

PLANTER BOX

REFER BELOW DETAILS FOR PLANTER BOX.



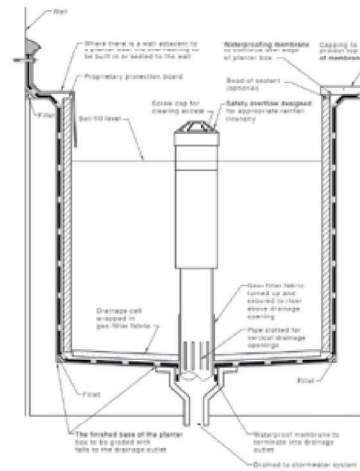


FIGURE 2.17 TYPICAL PLANTER BOX CONSTRUCTION

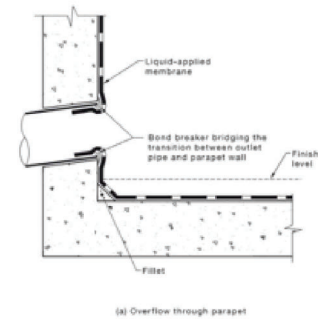

OVERFLOW TO BALCONY:

- SURFACE DRAIN & C/VERFLOW TO BALCONY

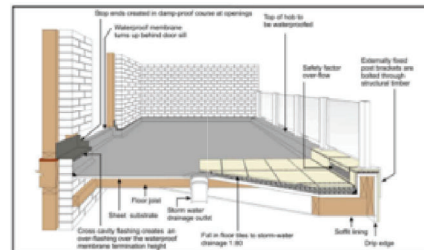

SWIMMING POOL

- PART 12.1.1 (H7D2) OF THE NCC VOLUME 2, AMENDMENT 1 - BUILDING CODE OF AUSTRALIA 2022 & HOUSING PROVISIONS STANDARD 2022
- AS 1926 PART 1-2012 – SWIMMING POOLSAFETY- SAFETY BARRIERS FOR SWIMMING POOLS
- AS 1926 PART 2-2007 - SWIMMING POOL SAFETY- LOCATION OF SAFETY BARRIERS FOR SWIMMING POOLS (INCORPORATING AMENDMENTS 1 AND 2)
- AS 1926 PART 3-2010 – SWIMMING POOL SAFETY- WATER RECIRCULATION SYSTEMS (INCORPORATING AMENDMENT 1)

OnBuild Certifiers Pty Ltd

Reference: 260016

Date: 16/04/2026

Andrew Soliman

Director/ Principal Certifier

BDC2940

Consultant who prepared this document remains responsible for accuracy

REV	DATE	DESCRIPTION	BY
3	3-02-2026	CDC ISSUE	
1	9-12-2025	Living & Alfresco extended to increase 5 sqm by Nava	



RUBY HOMES

THIS DRAWING IS THE EXCLUSIVE PROPERTY OF THE DEVELOPER & THE REPRODUCTION OF ANY PART WITHOUT THE PRIOR WRITTEN CONSENT OF THE DEVELOPER IS A VIOLATION OF APPLICABLE LAWS. IN NO EVENT SHALL THE DEVELOPER BE HELD LIABLE FOR SPECIAL, COLLATERAL, INCIDENTAL OR CONSEQUENTIAL LIABILITY IN CONNECTION WITH THE USE OF THIS DIGITAL DATA ONCE RELEASED FROM THE DEVELOPERS OFFICE. THIS DRAWING IS TO BE READ & UNDERSTOOD IN CONJUNCTION WITH THE STRUCTURAL, MECHANICAL, ELECTRICAL & / OR ANY OTHER CONSULTANTS DOCUMENTATION AS MAY BE APPLICABLE TO THE PROJECT PRIOR TO THE START OF ANY WORKS AND FOR ITS DURATION.

PROJECT:
LOT 114 47 TWELFTH AVENUE
47 TWELFTH AVENUE
AUSTRAL

DRAWING TITLE:
GENERAL NOTES B

NORTH:

LOT NO:

114

DRAWN BY:

AS

DRAFTED BY:

SL

DATE:

15-04-2026

CHECKED BY:

RH

CLIENT NAME:

Abi Maharjan & Nikki Manandhar

SCALE:

1 : 2

CDC ISSUE


DRAWING No:

REV: 3


ISSUED BY:

CDC.02B

OnBuild Certifiers Pty Ltd
Reference: 260016
Date: 16/04/2026
Andrew Soliman
Director/ Principal Certifier
BDC2940
Consultant who prepared this document
remains responsible for accuracy

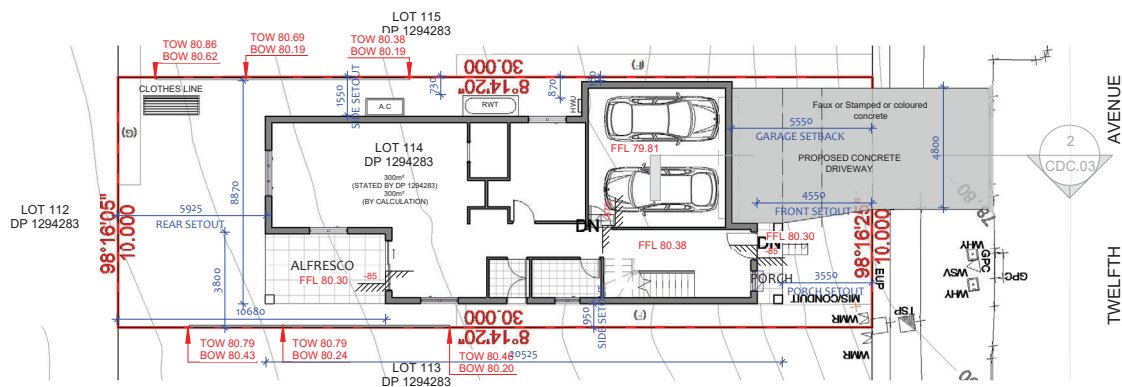

1 CDC - SITE PLAN
1 : 200

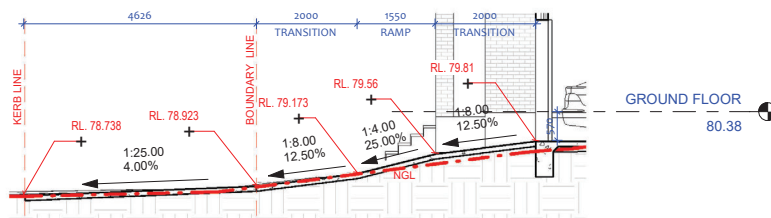

2 DRIVEWAY SECTION
1 : 100

GREENFIELD HOUSING CODE COMPLIANCE TABLE

DESCRIPTION		COMPLIANCE		COMMENT
ELEMENT	CODE CONTROL	REQUIREMNT	PROPOSED	
LAND ZONE	1 GENERAL RESIDENTIAL			
LOT NO	LOT 114			
LOT AREA	300 m2			
LOT WIDTH	Standard Lot Min. 6m at Building Line facing primary road	6.0m	10 m	YES
HEIGHT	MAX. Height	8.5m	7.6m (MAX.)	YES
FRONT SETBACK	FRONT SET BACK (Min. Setback from Primary Road) For 300-350 sqm. Lot	4.5 m	4.5m	YES
REAR SET BACK (MIN.)	GROUND FLOOR	3m	5.9 m	YES
	FIRST FLOOR	6m	10.6 m	
SIDE SET BACK (MIN.)	GROUND FLOOR	0/0.9m	0.1/0.95m	YES
	FIRST FLOOR	1.2/0.9m	1.5/0.95m	
FLOOR SPACE RATIO (FSR)	75% Of Lot Area	225.00m2	194 m2	YES
GROSS FLOOR AREA PLAN	GROUND FLOOR		93 m2	
	FIRST FLOOR		88 m2	
TOTAL FLOOR AREA			194 m2	
ROOF AREA			200 m2	
GARAGE			31 m2	
PRIVATE OPEN SPACE	<=10m Lot width	16m2	16m2	YES
LANDSCAPE AREA	10% of TOTAL LAND AREA	30 m2	73.95 m2	YES

3	3-02-2026	CDC ISSUE	
1	9-12-2025	Living & Alfresco extended to increase 5 sqm by Nava	
REV	DATE	DESCRIPTION	BY


RUBY HOMES

THIS DRAWING IS THE EXCLUSIVE PROPERTY OF THE DEVELOPER & THE REPRODUCTION OF ANY PART WITHOUT THE PRIOR WRITTEN CONSENT OF THE DEVELOPER IS A VIOLATION OF APPLICABLE LAWS. IN NO EVENT SHALL THE DEVELOPER BE HELD LIABLE FOR SPECIAL, COLLATERAL, INCIDENTAL OR CONSEQUENTIAL LIABILITY IN CONNECTION WITH THE USE OF THIS DIGITAL DATA ONCE RELEASED FROM THE DEVELOPER'S OFFICE. THIS DRAWING IS TO BE READ & UNDERSTOOD IN CONJUNCTION WITH THE STRUCTURAL, MECHANICAL, ELECTRICAL &/OR ANY OTHER CONSULTANT'S DOCUMENTATION AS MAY BE APPLICABLE TO THE PROJECT PRIOR TO THE START OF ANY WORKS AND FOR ITS DURATION.

PROJECT:
LOT 114 47 TWELFTH AVENUE
47 TWELFTH AVENUE
AUSTRAL


DRAWING TITLE:
LOCATION PLAN AND SITE PLAN



LOT NO:	114	DATE:	15-04-2026	SCALE:	As indicated	DRAWING No:	CDC.03	REV:	3
DRAWN BY:	AS	CHECKED BY:	RH					ISSUED BY:	
DRAFTED BY:	SL	CLIENT NAME:	Abi Maharjan & Nikki Manandhar						



- 1) STRIP TOPSOIL AND LEVEL SITE.
- 2) COMPACT SUBGRADE.
- 3) COVER AREA WITH GEOTEXILE.
- 4) CONSTRUCT 200 mm THICK PAD OVER GEOTEXILE USING ROADBASE OR 30 mm AGGREGATE. Min 15 m LONG OR TO BUILDING ALIGNMENT. Min 3 m WIDE.
- 5) CONSTRUCT HUMP IMMEDIATELY WITHIN BOUNDARY TO DIVERT WATER TO A SEDIMENT FENCE OR OTHER SEDIMENT TRAP.

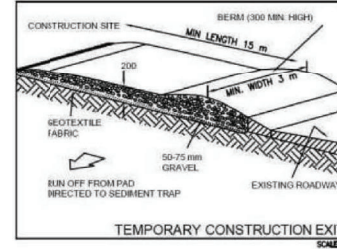

TEMPORARY 18M HIGH WIRE ML
FENCE WITH DUSTPROOF MESH
APPLIED TO FULL HEIGHT TO
BOUNDARIES AS REQUIRED

LOCATION OF WASTE BINS

SEDIMENT FENCE AS REQUIRED

GRAVEL ACCESS

SITE ACCESS AREA TO BE USED FOR
WASHDOWN AREA

FOOTPATH CLEAN AND CLEAR AT ALL
TIMES

LOCATION OF STOCKPILE MATERIAL

MATERIAL STORAGE AREA

TEMPORARY TOILETS

INSTALL TEMPORARY SEDIMENT
BARRIERS TO ALL INLET PITS LIKELY
TO COLLECT SILT LADEN WATER, TO
COUNCIL'S REQUIREMENTS.

- 1) FABRICATE A SEDIMENT BARRIER MADE FROM GEOTEXILE.
REFER SD6-7 FOR DETAILS.
- 2) SUPPORT GEOTEXILE WITH MESH TIED TO POSTS AT 1 m Ctrs.
- 3) DO NOT COVER INLET WITH GEOTEXILE.

1. ORIGIN OF LEVELS PROVIDED BY SURVEYOR
2. THE BUILDER SHALL VERIFY ALL DIMENSIONS AND EXISTING LEVELS ON SITE PRIOR TO THE COMMENCEMENT OF WORK AND ANY DISCREPANCIES SHALL BE REPORTED TO THE SURVEYOR / ENGINEER .
3. TOPSOIL SHALL BE STRIPPED FROM THE CONSTRUCTION AREA AND STOCKPILED ON SITE , TO BE REITER SPREAD OR DISPOSED OFF SITE , AS DIRECTED BY SUPERVISOR/ENGINEER.
4. ALL TH TRENCH BACKFILL MATERIAL SHALL BE COMPACTED TO THE SAME DENSITY AS THE ADJACENT MATERIAL.
5. ALL SERVICE TRENCHES UNDER VEHICULAR PAVEMENTS SHALL BE BACKFILLED WITH SAND OR APPROVED GRANULAR MATERIALS. TO THE SATISFACTION OF THE PAYOR. THE BACKFILL SHALL BE COMPACTED TO 98% STANDARD MAXIMUM DRY DENSITY, IN ACCORDANCE WITH AS 1289E.1.

SEDIMENT AND EROSION NOTES

THIS PLAN IS TO BE READ IN CONJUNCTION WITH SEDIMENT AND EROSION CONTROL DETAILS AS ATTACHED.

THE CONTRACTOR SHALL IMPLEMENT ALL SOIL EROSION AND SEDIMENT CONTROL MEASURES AS NECESSARY AND TO THE SATISFACTION OF COUNCIL PRIOR TO THE COMMENCEMENT AND DURING CONSTRUCTION.

NO DISTURBANCE TO THE SITE SHALL BE PERMITTED OTHER THAN IN THE IMMEDIATE AREA OF THE WORK AND NO MATERIAL SHALL BE REMOVED FROM THE SITE WITHOUT COUNCIL'S APPROVAL.

ALL SEDIMENT AND EROSION CONTROL DEVICES TO BE INSTALLED AND MAINTAINED IN

- TOPSOIL SHALL BE STRIPPED AND STOCKPILED OUTSIDE HAZARD AREAS SUCH AS DRAINAGE LINES. THIS TOP SOIL IS TO BE RESPIRED LATER ON AREAS TO BE REVEGETATED AND STABILISED ONLY. (I.E ALL FOOTPATHS,BATTERS,SITE REGARDING AREAS,BASINS AND CATCH DRAINS),TOPSOIL SHALL NOT BE RESPIRED ON ANY OTHER AREAS UNLESS SPECIALLY INSTRUCTED BY THE SUPERIDENT.IF THEY ARE TO REMAIN FOR LONGER THAN ONE MONTH STOCKPILES SHALL BE PROTECTED FROM EROSION BY COVERING THEM WITH A MULCH AND HYDROSEEDING AND,IF NECESSARY,BY LOCATING BANKS OR DRAINS DOWNSTREAM OF A STOCKPILE TO RETARD SILT LADEN RUNOFF.
- THE CONTRACTOR SHALL REGULARLY MAINTAIN ALL SEDIMENT AND EROSION CONTROL DEVICES AND REMOVE ACCUMULATED SILT FROM SUCH DEVICES SUCH THAT MORE THAN 60% OF THEIR CAPACITY LOST.ALL THE SILTS TO BE PLACED OUTSIDE THE LIMIT OF WORKS.THE PERIOD FOR MAINTAINING THESE DEVICES SHALL BE AT LEAST UNTIL ALL DISTURBED AREAS ARE REVEGETATED AND FURTHER AS MAY BE DIRECTED BY THE SUPERINTENDENT OR COUNCIL.
- LAY TURF STRIP (MIN 300 mm WIDE) ON 100 mm TOPSOIL WITH 1.0 m LONG RETURNS EVERY 6.0m INCLUDING ALL KERB AT THE TOP OF ALL BATTERS AND AROUND STRUCTURES IMMEDIATELY AFTER BACKFILLING OR FORMATION.
- THE CONTRACTOR SHALL GRASS SEED ALL DISTURBED AREAS WITH AN APPROVED MIX AS SSON AS PRACTICABLE AFTER COMPLETION OF EARTHWORKS AND REGRADING.
- VEHICULAR TRAFFIC SHALL BE CONTROLLED DURING CONSTRUCTION CONFINING ACCESS WHERE POSSIBLE TO NOMINATED STABILISED ACCESS POINTS.
- WHEN ANY DEVICES ARE TO BE HANDED OVER TO COUNCIL,THEY SHALL BE IN CLEAN AND STABLE CONDITION.
- THE CONTRACTOR SHALL IMPLEMENT DUST CONTROL BY REGULAR WETTING DOWN(BUT NOT SATURATING) DISTURBED AREA.
- PROVIDE AND MAINTAIN SILT TRAPS AROUND ALL SURFACE INLET PITS UNTL CATCHMENT IS REVEGETATED OR PAVED.
- REVEGETATE ALL TRENCHES IMMEDIATELY UPON COMPLETION OF BACKFILLING.
- ALL DRAINAGE PIPE INLETS TO BE CAPPED UNTIL:
 - A) DOWNPIPES CONNECTED
 - B) PITS CONSTRUCTED & PROTECTED WITH SILT BARRIER

- 1) FABRICATE A SEDIMENT BARRIER MADE FROM GEOTEXILE. REFER SD6-7 FOR DETAILS.
- 2) SUPPORT GEOTEXILE WITH MESH TIED TO POSTS AT 1 m Ctrs.
- 3) DO NOT COVER INLET WITH GEOTEXILE.



THIS DRAWING IS THE EXCLUSIVE PROPERTY OF THE DEVELOPER AND THE REPRODUCTION OF ANY PART WITHOUT THE PRIOR WRITTEN CONSENT OF THE DEVELOPER IS A VIOLATION OF APPLICABLE LAWS. IN NO EVENT SHALL THE DEVELOPER BE HELD LIABLE FOR SPECIAL, COLLATERAL, INCIDENTAL OR CONSEQUENTIAL LIABILITY IN CONNECTION WITH THE USE OF THIS DIGITAL DATA ONCE RELEASED FROM THE DEVELOPERS OFFICE. THIS DRAWING IS TO BE READ & UNDERSTOOD IN CONJUNCTION WITH THE STRUCTURAL, MECHANICAL, ELECTRICAL AND ALL OTHER CONSULTANT DOCUMENTATION AND MAY BE APPLICABLE TO THE PROJECT PRIOR TO THE START OF ANY WORKS


DRAWING TITLE:
**SITE ANALYSIS
AND SEDIMENT
CONTROL PLAN**



LOT NO:	DATE:	SCALE:	DRAWING No:	REV:
114	15-04-2026	1 : 200	CDC.04	3
DRAWN BY:	CHECKED BY:			ISSUED BY:
AS	RH			
DRAFTED BY:	CLIENT NAME:			
SL	Abi Maharian & Nikki Manandhar			

OnBuild Confidential Ltd
Reference: 114
Date: 15-04-2026
Andrew Mahajan
Director/ Principal Designer
BDP 06240
Consultant who prepared this document remains responsible for the accuracy of the information provided.

IMPORTANT NOTES
ALL DIMENSIONS AND NOTES ON ALL PLANS MUST BE CHECKED AND VERIFIED BY BUILDERS AND OWNER PRIOR TO COMMENCEMENT OF ANY BUILDING WORKS. TO CLARIFY AND CONFIRM WITH THE CONSTRUCTION COMPANY FOR DISCREPANCIES ON ALL DOCUMENTS AND PLANS PROVIDED FOR CONSTRUCTION ANY WORK INDICATED ON THE PLAN BUT NOT IN CONTRACT VARIATION TO PLANS. SPECIFICATIONS MAY NOT BE THE RESPONSIBILITY OF THE BUILDING END USER TO VERIFY PLANS CURRENT BCA AND AUSTRALIAN STANDARDS. WINDOWS TO COMPLY WITH 3.9.3.5 OF THE BCA. ARCHITECT PLAN TO BE IN ACCORDANCE WITH NCC VOLUME 2 BUILDING CODE OF AUSTRALIA 2022 & HOUSING PROVISIONS STANDARD 2022.

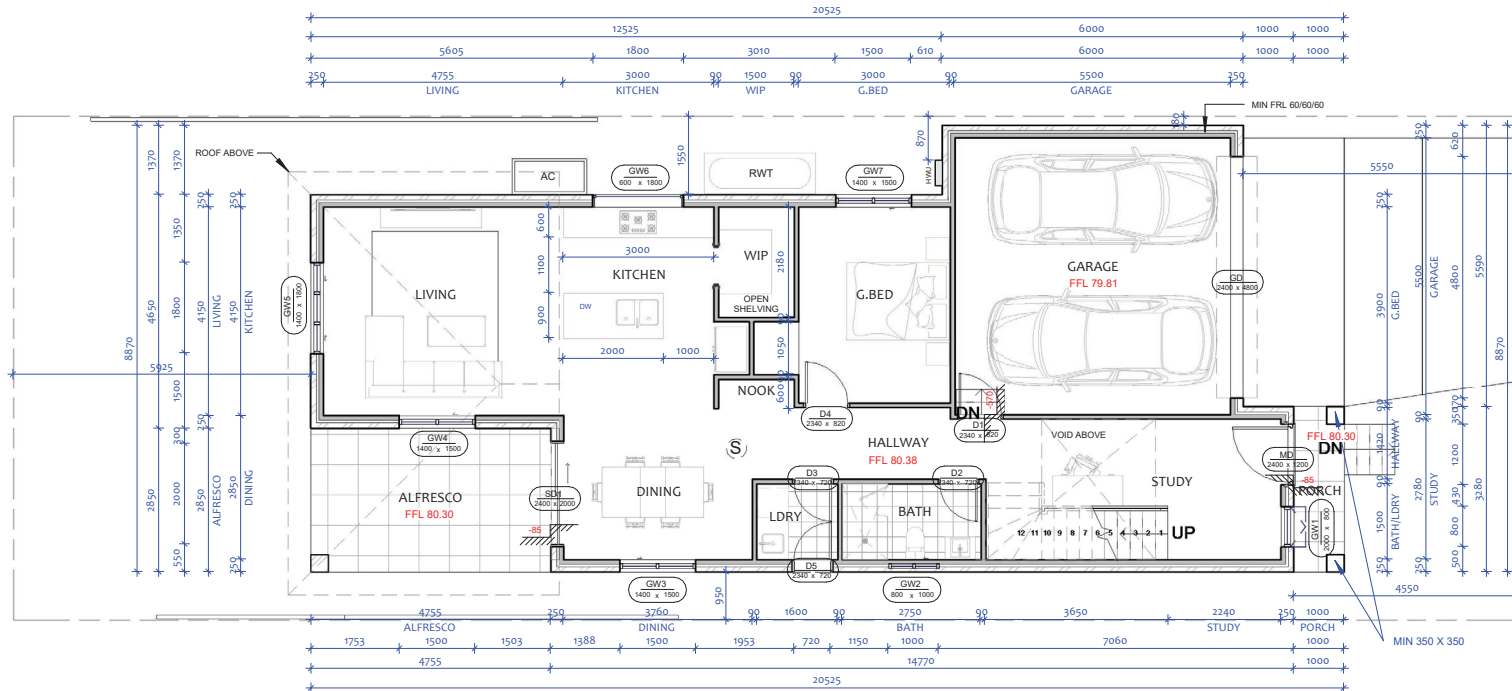

1 GROUND FLOOR PLAN
1 : 100

REV	DATE	DESCRIPTION	BY
3	3-02-2026	CDC ISSUE	
2	11-12-2025	Sliding door to dining & Window to Living at alfresco - Nava,puja	
1	9-12-2025	Living & Alfresco extended to increase 5 sqm by Nava	


RUBY HOMES

THIS DRAWING IS THE EXCLUSIVE PROPERTY OF THE DEVELOPER & THE REPRODUCTION OF ANY PART WITHOUT THE PRIOR WRITTEN CONSENT OF THE DEVELOPER IS A VIOLATION OF APPLICABLE LAWS. IN NO EVENT SHALL THE DEVELOPER BE HELD LIABLE FOR SPECIAL COLLATERAL, INCIDENTAL OR CONSEQUENTIAL LIABILITY IN CONNECTION WITH THE USE OF THIS DIGITAL DATA ONCE RELEASED FROM THE DEVELOPER'S OFFICE. THIS DRAWING IS TO BE READ & UNDERSTOOD IN CONJUNCTION WITH THE STRUCTURAL, MECHANICAL, ELECTRICAL & / OR ANY OTHER CONSULTANT'S DOCUMENTATION AS MAY BE APPLICABLE TO THE PROJECT PRIOR TO THE START OF ANY WORKS AND FOR ITS DURATION.

PROJECT:
LOT 114 47 TWELFTH AVENUE
47 TWELFTH AVENUE
AUSTRAL


DRAWING TITLE:
GROUND FLOOR PLAN



LOT NO:	DATE:	SCALE:	DRAWING No:	REV:
114	15-04-2026	1 : 100	CDC.05	3
DRAWN BY:	CHECKED BY:	CLIENT NAME:	ISSUED BY:	
AS	RH	Abi Maharjan & Nikki Manandhar		
DRAFTED BY:	SL			

OnBuild Confidential Ltd
Reference: 114
Date: 15-04-2026
Andrew Mahajan
Director/ Principal Designer
BD 996240
Consultant who prepared this document remains responsible for the accuracy of the information provided.

IMPORTANT NOTES
ALL DIMENSIONS AND NOTES ON ALL PLANS MUST BE CHECKED AND VERIFIED BY BUILDERS AND OWNER PRIOR TO COMMENCEMENT OF ANY BUILDING WORKS. TO CLARIFY AND CONFIRM WITH THE CONSTRUCTION COMPANY FOR DISCREPANCIES ON ALL DOCUMENTS AND PLANS PROVIDED FOR CONSTRUCTION ANY WORK INDICATED ON THE PLAN BUT NOT IN CONTRACT VARIATION TO PLANS. SPECIFICATIONS MAY NOT BE RESPONSIBILITY OF THE BUILDER/END USER TO VERIFY PLANS CURRENT BCA AND AUSTRALIAN STANDARDS. WINDOWS TO COMPLY WITH 3.9.3.5 OF THE BCA. ARCHITECT PLAN TO BE IN ACCORDANCE WITH NCC VOLUME 2 BUILDING CODE OF AUSTRALIA 2022 & HOUSING PROVISIONS STANDARD 2022.

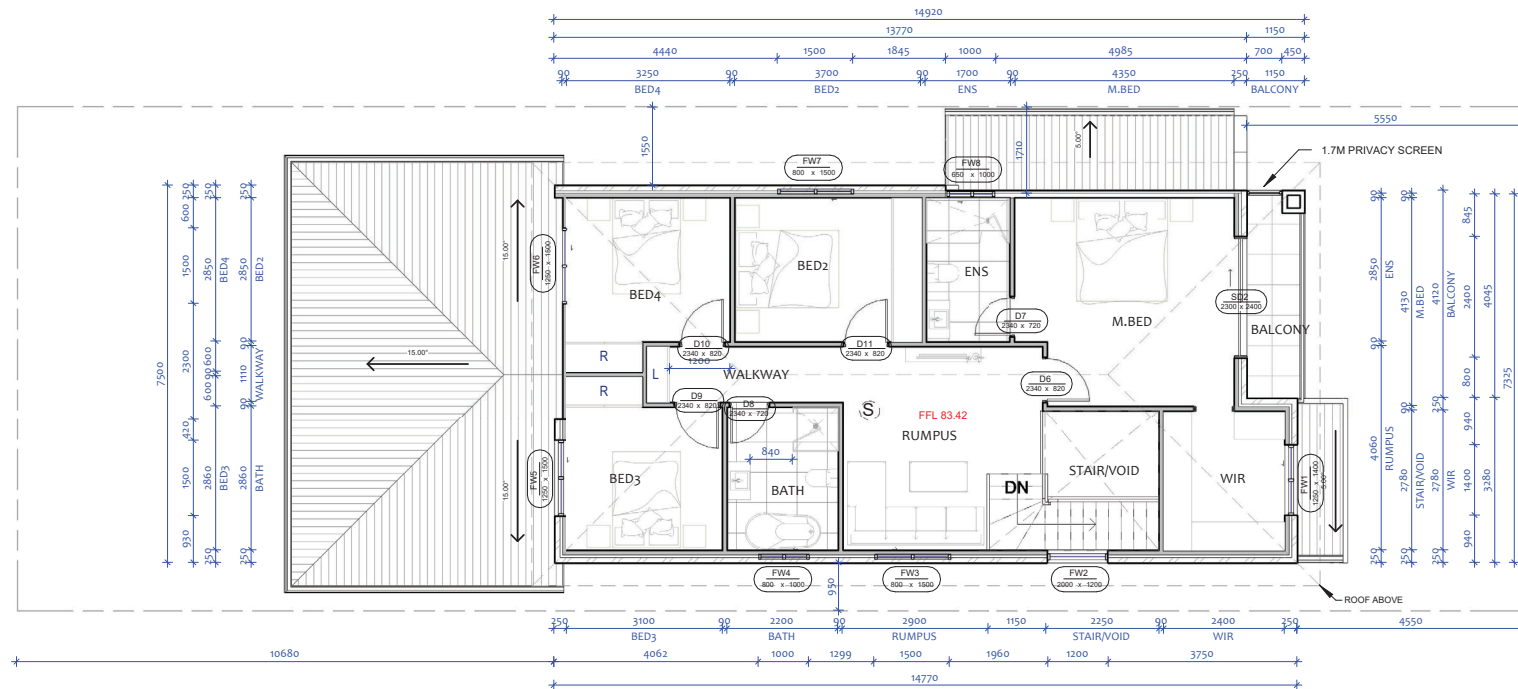

1 FIRST FLOOR PLAN
1 : 100

REV	DATE	DESCRIPTION	BY
3	3-02-2026	CDC ISSUE	
1	9-12-2025	Living & Alfresco extended to increase 5 sqm by Nava	

RUBY HOMES

THIS DRAWING IS THE EXCLUSIVE PROPERTY OF THE DEVELOPER & THE REPRODUCTION OF ANY PART WITHOUT THE PRIOR WRITTEN CONSENT OF THE DEVELOPER IS A VIOLATION OF APPLICABLE LAWS. IN NO EVENT SHALL THE DEVELOPER BE HELD LIABLE FOR SPECIAL, COLLATERAL, INCIDENTAL OR CONSEQUENTIAL LIABILITY IN CONNECTION WITH THE USE OF THIS DIGITAL DATA ONCE RELEASED FROM THE DEVELOPER'S OFFICE. THIS DRAWING IS TO BE READ & UNDERSTOOD IN CONJUNCTION WITH THE STRUCTURAL, MECHANICAL, ELECTRICAL & / OR ANY OTHER CONSULTANT'S DOCUMENTATION AS MAY BE APPLICABLE TO THE PROJECT PRIOR TO THE START OF ANY WORKS AND FOR ITS DURATION.

PROJECT:
LOT 114 47 TWELFTH AVENUE
47 TWELFTH AVENUE AUSTRAL


DRAWING TITLE:
FIRST FLOOR PLAN



LOT NO:	DATE:	SCALE:	DRAWING No:	REV:
114	15-04-2026	1 : 100	CDC.06	3
DRAWN BY: AS	CHECKED BY: RH			ISSUED BY:
DRAFTED BY: SL	CLIENT NAME: Abi Maharjan & Nikki Manandhar			

OnBuild Construction Ltd
Reference: BDC 2025/001
Date: 15-04-2026
Andrew Mahajan
Director/ Principal Designer
BDC 2025/001
Consultant who prepared this document remains responsible for the design.

IMPORTANT NOTES
ALL DIMENSIONS AND NOTES ON ALL PLANS MUST BE CHECKED AND VERIFIED BY BUILDERS AND OWNER PRIOR TO COMMENCEMENT OF ANY BUILDING WORKS. TO CLARIFY AND CONFIRM WITH THE CONSTRUCTION COMPANY FOR DISCREPANCIES ON ALL DOCUMENTS AND PLANS PROVIDED FOR CONSTRUCTION ANY WORK INDICATED ON THE PLAN BUT NOT IN CONTRACT VARIATION TO PLANS. SPECIFICATIONS MAY NOT BE THE RESPONSIBILITY OF THE BUILDING END USER TO VERIFY PLANS CURRENT BCA AND AUSTRALIAN STANDARDS. WINDOWS TO COMPLY WITH 3.9.3.5 OF THE BCA. ARCHITECT PLAN TO BE IN ACCORDANCE WITH NCC VOLUME 2 BUILDING CODE OF AUSTRALIA 2022 & HOUSING PROVISIONS STANDARD 2022.

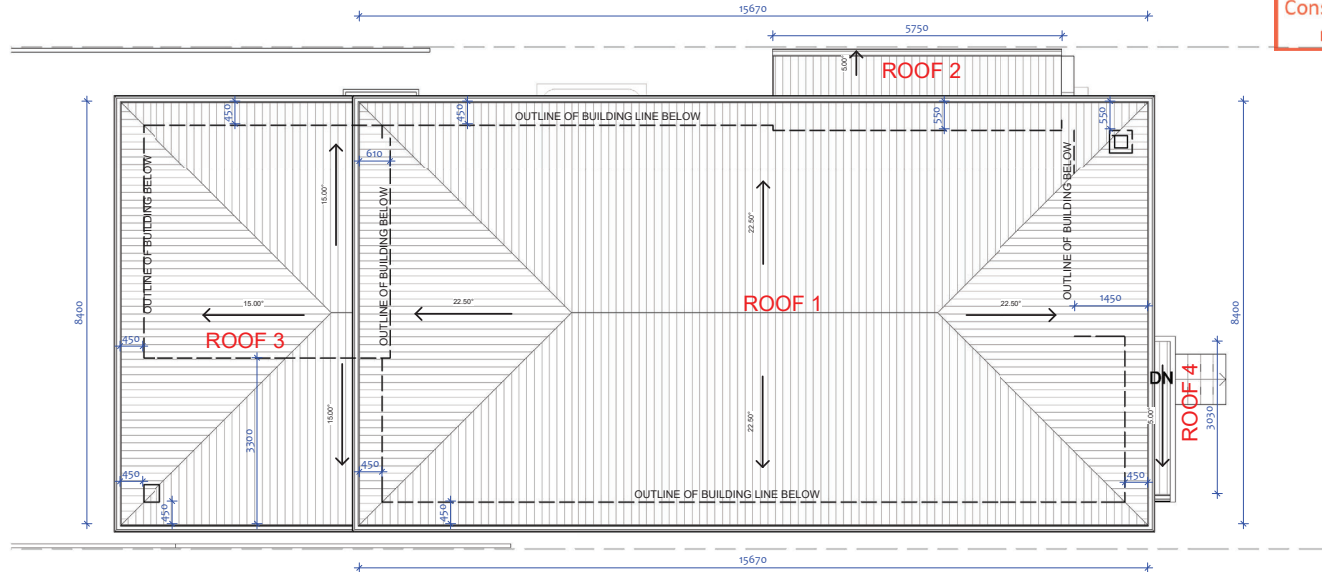

1 ROOF PLAN CDC

1 : 100

Roof Schedule		
Mark	Area	Comments
ROOF 2	8.83 m ²	COLORBOND(Black or shades of grey or neutral colours only - Non reflective corrugated roof)
ROOF 3	46.23 m ²	COLORBOND(Black or shades of grey or neutral colours only - Non reflective corrugated roof)
ROOF 4	2.74 m ²	COLORBOND(Black or shades of grey or neutral colours only - Non reflective corrugated roof)
GROUND FLOOR CEILING: 3	57.79 m ²	
ROOF 1	142.47 m ²	COLORBOND(Black or shades of grey or neutral colours only - Non reflective corrugated roof)
FIRST FLOOR CEILING: 1	142.47 m ²	
Grand total	200.27 m ²	

REV	DATE	DESCRIPTION	BY
3	3-02-2026	CDC ISSUE	
1	9-12-2025	Living & Alfresco extended to increase 5 sqm by Nava	




RUBY HOMES


THIS DRAWING IS THE EXCLUSIVE PROPERTY OF THE DEVELOPER & THE REPRODUCTION OF ANY PART WITHOUT THE PRIOR WRITTEN CONSENT OF THE DEVELOPER IS A VIOLATION OF APPLICABLE LAWS. IN NO EVENT SHALL THE DEVELOPER BE HELD LIABLE FOR SPECIAL, COLLATERAL, INCIDENTAL OR CONSEQUENTIAL LIABILITY IN CONNECTION WITH THE USE OF THIS DIGITAL DATA ONCE RELEASED FROM THE DEVELOPER'S OFFICE. THIS DRAWING IS TO BE READ & UNDERSTOOD IN CONJUNCTION WITH THE STRUCTURAL, MECHANICAL, ELECTRICAL & / OR ANY OTHER CONSULTANT'S DOCUMENTATION AS MAY BE APPLICABLE TO THE PROJECT PRIOR TO THE START OF ANY WORKS AND FOR ITS DURATION.

PROJECT:
LOT 114 47 TWELFTH AVENUE
47 TWELFTH AVENUE
AUSTRAL


DRAWING TITLE:
ROOF PLAN

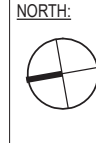

LOT NO:	DATE:	SCALE:	DRAWING No:	REV:
114	15-04-2026	1 : 100	CDC.07	3
DRAWN BY:	CHECKED BY:			ISSUED BY:
AS	RH			
DRAFTED BY:	CLIENT NAME:			
SL	Abi Maharjan & Nikki Manandhar			

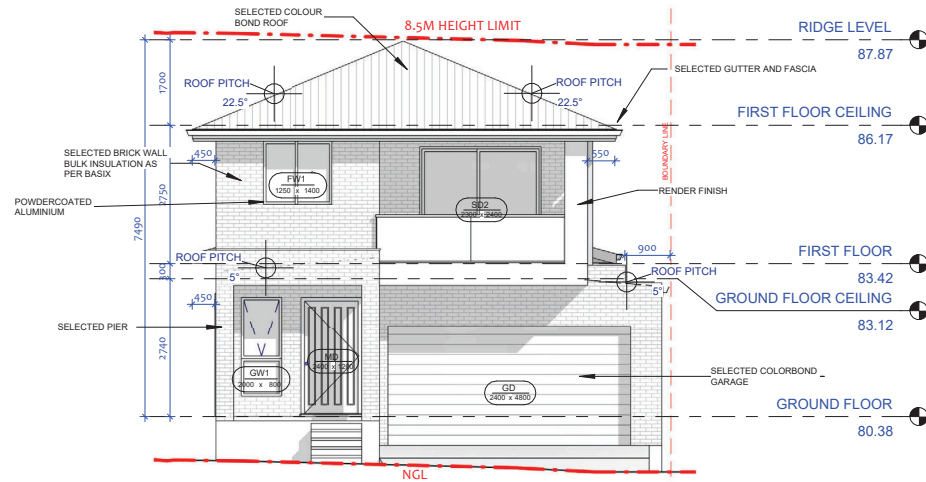

2 SOUTH ELEVATION
1 : 100

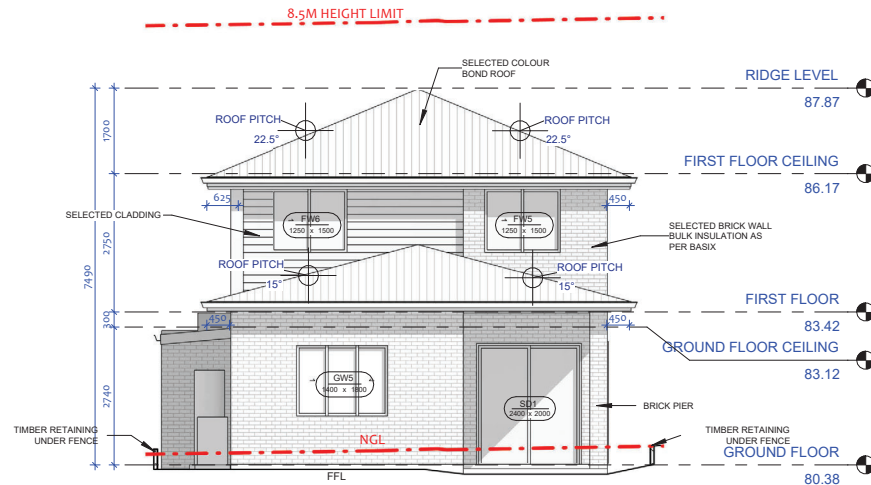

1 NORTH ELEVATION
1 : 100

Window Schedule 1					
Mark	Height	Width	Sill Height	Head Height	Description

GROUND FLOOR

GW1	2000	800	400	2400	AWNING
GW2	800	1000	1000	2400	SLIDING
GW3	1400	1500	1000	2400	SLIDING
GW4	1400	1500	1000	2400	SLIDING
GW5	1400	1800	1000	2400	SLIDING
GW6	600	1800	950	1550	FIXED
GW7	1400	1500	1000	2400	SLIDING

GROUND FLOOR: 7

FIRST FLOOR

FW1	1250	1400	1200	2450	SLIDING
FW2	2000	1200	450	2450	FIXED
FW3	800	1500	1650	2450	SLIDING
FW4	800	1000	1650	2450	SLIDING
FW5	1250	1500	1200	2450	SLIDING
FW6	1250	1500	1200	2450	SLIDING
FW7	800	1500	1650	2450	SLIDING
FW8	650	1000	1800	2450	SLIDING

FIRST FLOOR: 8

Door Schedule 1				
Mark	Height	Width	Count	Description

GROUND FLOOR

D1	2340	820	1	FLUSH DOOR
D2	2340	720	1	FLUSH DOOR
D3	2340	720	1	FLUSH DOOR
D4	2340	820	1	FLUSH DOOR
D5	2340	720	1	FLUSH DOOR
GD	2400	4800	1	GARAGE DOOR
MD	2400	1200	1	SOLID CORE DOOR
SD1	2400	2000	1	SLIDING DOOR

GROUND FLOOR: 8

FIRST FLOOR

D6	2340	820	1	FLUSH DOOR
D7	2340	720	1	FLUSH DOOR
D8	2340	720	1	FLUSH DOOR
D9	2340	820	1	FLUSH DOOR
D10	2340	820	1	FLUSH DOOR
D11	2340	820	1	FLUSH DOOR
SD2	2300	2400	1	SLIDING DOOR

FIRST FLOOR: 7

OnBuild Certifiers Pty Ltd
Reference: 260016
Date: 16/04/2026
Andrew Soliman
Director/ Principal Certifier
BDC2940

consultant who prepares this document remains responsible for accuracy

REV	DATE	DESCRIPTION	BY
3	3-02-2026	CDC ISSUE	
1	9-12-2025	Living & Alfresco extended to increase 5 sqm by Nava	

RUBY HOMES

THIS DRAWING IS THE EXCLUSIVE PROPERTY OF THE DEVELOPER & THE REPRODUCTION OF ANY PART WITHOUT THE PRIOR WRITTEN CONSENT OF THE DEVELOPER IS A VIOLATION OF APPLICABLE LAWS. IN NO EVENT SHALL THE DEVELOPER BE HELD LIABLE FOR SPECIAL, COLLATERAL, INCIDENTAL OR CONSEQUENTIAL LIABILITY IN CONNECTION WITH THE USE OF THIS DIGITAL DATA ONCE RELEASED FROM THE DEVELOPERS OFFICE. THIS DRAWING IS TO BE READ & UNDERSTOOD IN CONJUNCTION WITH THE STRUCTURAL, MECHANICAL, ELECTRICAL & / OR ANY OTHER CONSULTANT'S DOCUMENTATION AS MAY BE APPLICABLE TO THE PROJECT PRIOR TO THE START OF ANY WORKS AND FOR ITS DURATION.


PROJECT:
LOT 114 47 TWELFTH AVENUE
47 TWELFTH AVENUE
AUSTRAL

DRAWING TITLE:
ELEVATIONS 01


NORTH:

LOT NO:	DATE:	SCALE:	DRAWING No:	REV:
114	15-04-2026	1 : 100	CDC.08	3
DRAWN BY:	CHECKED BY:			ISSUED BY:
AS	RH			
DRAFTED BY:	CLIENT NAME:			
SL	Abi Maharjan & Nikki Manandhar			

OnBuild Certifiers Pty Ltd
Reference: 260016
Date: 16/04/2026
Andrew Soliman
Director/ Principal Certifier
BDC2940
Consultant who prepared this document
remains responsible for accuracy

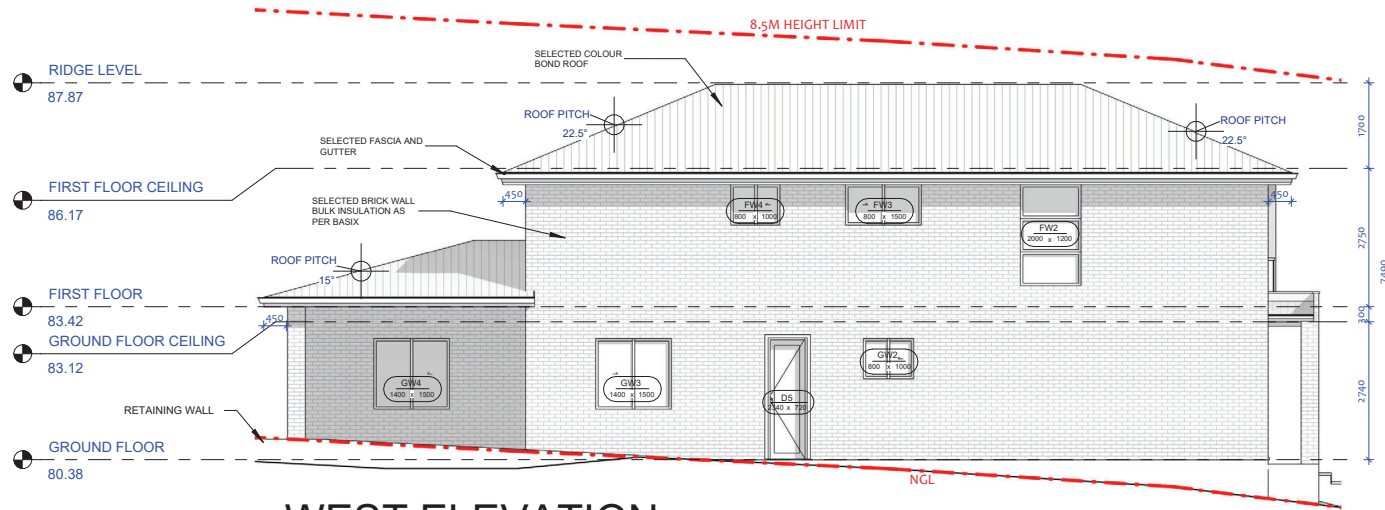

1 WEST ELEVATION
1 : 100

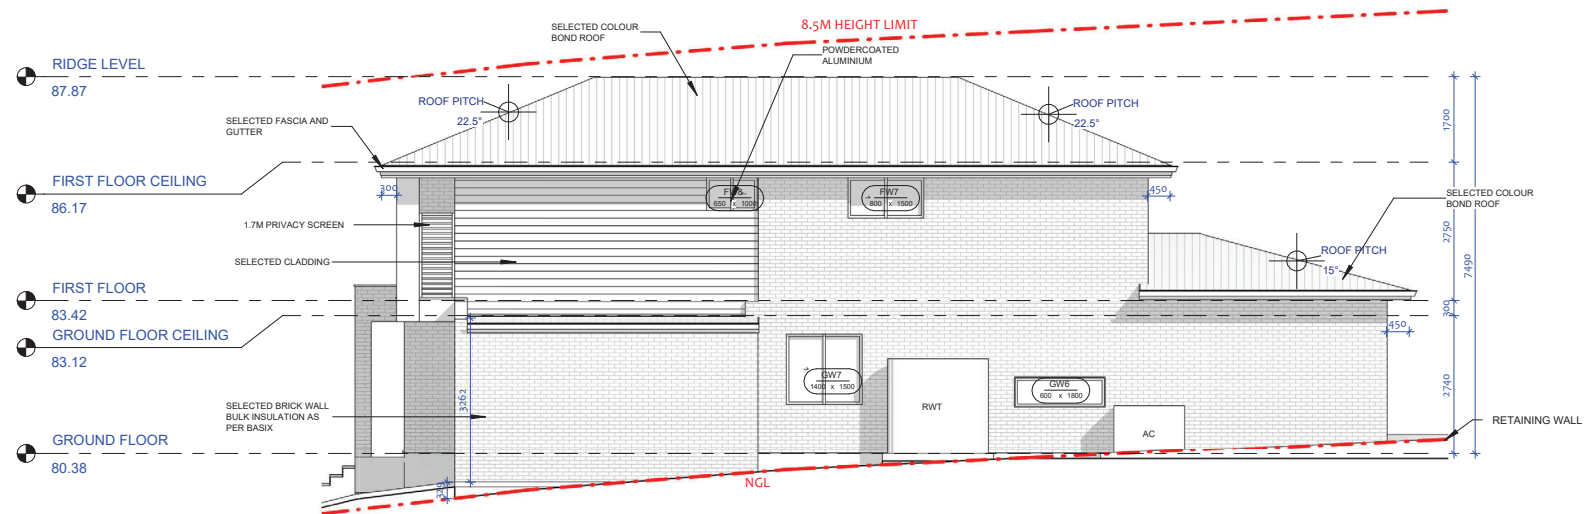

2 EAST ELEVATION
1 : 100

REV	DATE	DESCRIPTION	BY
3	3-02-2026	CDC ISSUE	
1	9-12-2025	Living & Alfresco extended to increase 5 sqm by Nava	


RUBY HOMES
THIS DRAWING IS THE EXCLUSIVE PROPERTY OF THE DEVELOPER & THE REPRODUCTION OF ANY PART WITHOUT THE PRIOR WRITTEN CONSENT OF THE DEVELOPER IS A VIOLATION OF APPLICABLE LAWS. IN NO EVENT SHALL THE DEVELOPER BE HELD LIABLE FOR SPECIAL, COLLATERAL, INCIDENTAL OR CONSEQUENTIAL LIABILITY IN CONNECTION WITH THE USE OF THIS DIGITAL DATA ONCE RELEASED FROM THE DEVELOPER'S OFFICE. THIS DRAWING IS TO BE READ & UNDERSTOOD IN CONJUNCTION WITH THE STRUCTURAL, MECHANICAL, ELECTRICAL & / OR ANY OTHER CONSULTANT'S DOCUMENTATION AS MAY BE APPLICABLE TO THE PROJECT PRIOR TO THE START OF ANY WORKS AND FOR ITS DURATION.

PROJECT:
LOT 114 47 TWELFTH AVENUE
47 TWELFTH AVENUE
AUSTRAL



DRAWING TITLE:
ELEVATIONS 02

NORTH:

LOT NO:	DATE:	SCALE:	DRAWING No:	REV:
114	15-04-2026	1 : 100	CDC.09	3
DRAWN BY:	CHECKED BY:			
AS	RH			
DRAFTED BY:	CLIENT NAME:			
SL	Abi Maharjan & Nikki Manandhar			

CDC ISSUE

OnBuild Certifiers Pty Ltd
Reference: 260016
Date: 16/04/2026
Andrew Soliman
Director/ Principal Certifier
BDC2940
Consultant who prepared this document
remains responsible for accuracy

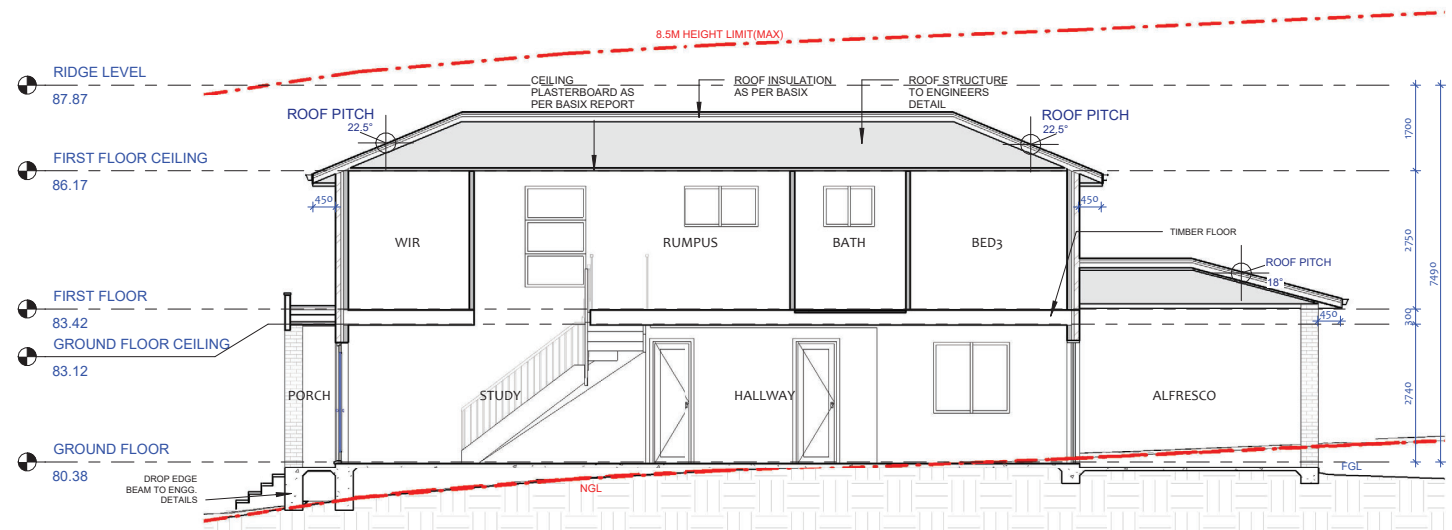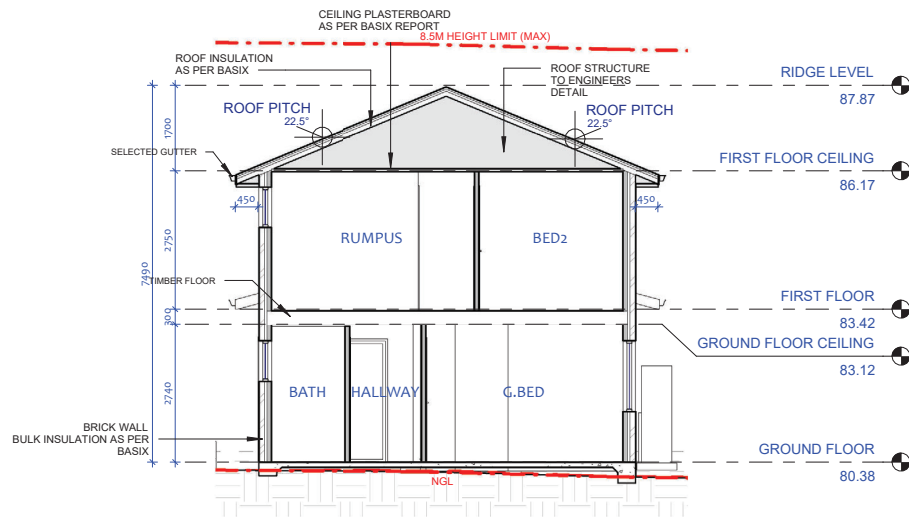

REV	DATE	DESCRIPTION	BY
3	3-02-2026	CDC ISSUE	
1	9-12-2025	Living & Alfresco extended to increase 5 sqm by Nava	

RUBY HOMES


THIS DRAWING IS THE EXCLUSIVE PROPERTY OF THE DEVELOPER & THE REPRODUCTION OF ANY PART WITHOUT THE PRIOR WRITTEN CONSENT OF THE DEVELOPER IS A VIOLATION OF APPLICABLE LAWS. IN NO EVENT SHALL THE DEVELOPER BE HELD LIABLE FOR SPECIAL, COLLATERAL, INCIDENTAL OR CONSEQUENTIAL LIABILITY IN CONNECTION WITH THE USE OF THIS DIGITAL DATA ONCE RELEASED FROM THE DEVELOPER'S OFFICE. THIS DRAWING IS TO BE READ & UNDERSTOOD IN CONJUNCTION WITH THE STRUCTURAL, MECHANICAL, ELECTRICAL &/OR ANY OTHER CONSULTANT'S DOCUMENTATION AS MAY BE APPLICABLE TO THE PROJECT PRIOR TO THE START OF ANY WORKS AND FOR ITS DURATION.

PROJECT:
LOT 114 47 TWELFTH AVENUE
47 TWELFTH AVENUE
AUSTRAL

DRAWING TITLE:
SECTIONS

NORTH:

LOT NO:	DATE:	SCALE:	DRAWING No:	REV:
114	15-04-2026	1 : 100	CDC.10	3
DRAWN BY:	CHECKED BY:	CLIENT NAME:	ISSUED BY:	
AS	RH	Abi Maharjan & Nikki Manandhar		
DRAFTED BY:				
SL				

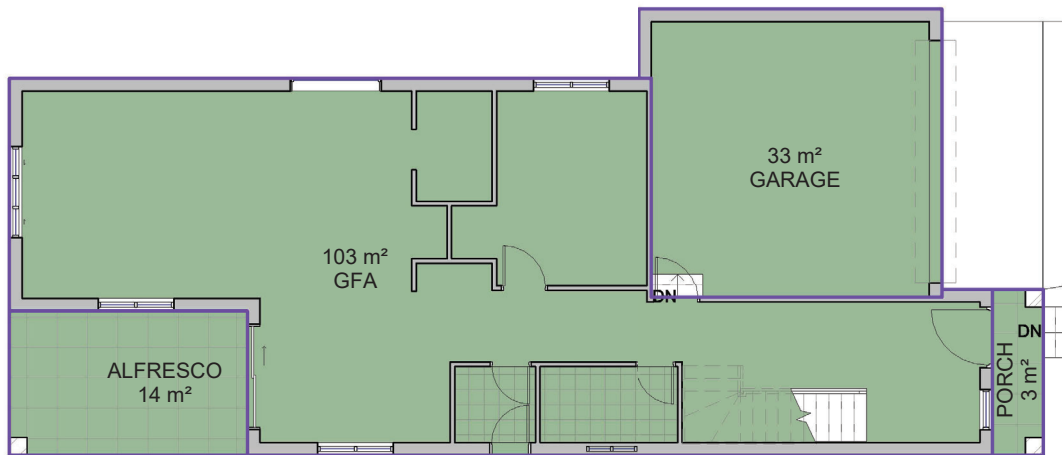

1 **GROUND FLOOR**
1 : 100

OnBuild Certifiers Pty Ltd
Reference: 260016
Date: 16/04/2026
Andrew Soliman
Director/ Principal Certifier
Area Schedule (Gross Building)
BDC2940
Consultant Name: [Redacted] Area: [Redacted]
[Redacted] prepared this document
[Redacted] remains responsible for accuracy

GROUND FLOOR

ALFRESCO	14 m²
GARAGE	33 m²
GFA	103 m²
PORCH	3 m²


GROUND FLOOR: 4 154 m²

FIRST FLOOR

BALCONY	5 m²
FFA	99 m²
VOID	8 m²

FIRST FLOOR: 3 111 m²

Grand total 265 m²

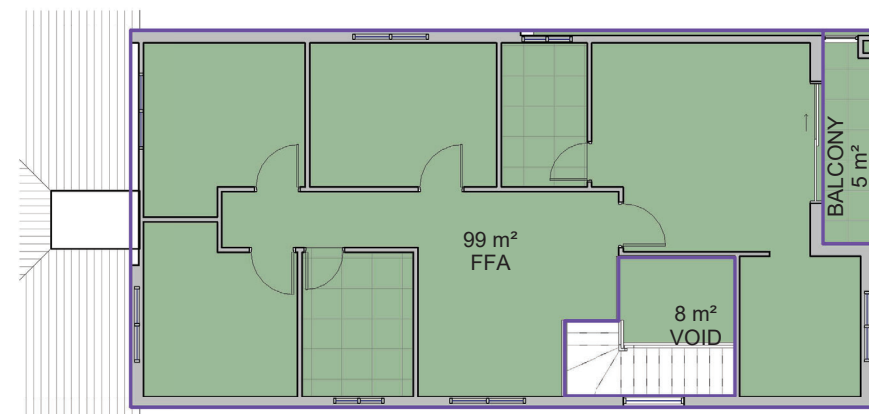

2 **FIRST FLOOR**
1 : 100


REV	DATE	DESCRIPTION	BY
3	3-02-2026	CDC ISSUE	
1	9-12-2025	Living & Alfresco extended to increase 5 sqm by Nava	

RUBY HOMES


THIS DRAWING IS THE EXCLUSIVE PROPERTY OF THE DEVELOPER & THE REPRODUCTION OF ANY PART WITHOUT THE PRIOR WRITTEN CONSENT OF THE DEVELOPER IS A VIOLATION OF APPLICABLE LAWS. IN NO EVENT SHALL THE DEVELOPER BE HELD LIABLE FOR SPECIAL, COLLATERAL, INCIDENTAL OR CONSEQUENTIAL LIABILITY IN CONNECTION WITH THE USE OF THIS DIGITAL DATA ONCE RELEASED FROM THE DEVELOPER'S OFFICE. THIS DRAWING IS TO BE READ & UNDERSTOOD IN CONJUNCTION WITH THE STRUCTURAL, MECHANICAL, ELECTRICAL &/OR ANY OTHER CONSULTANT'S DOCUMENTATION AS MAY BE APPLICABLE TO THE PROJECT PRIOR TO THE START OF ANY WORKS AND FOR ITS DURATION.

PROJECT:
LOT 114 47 TWELFTH AVENUE
47 TWELFTH AVENUE
AUSTRAL

DRAWING TITLE:
GROSS FLOOR
AREA PLAN

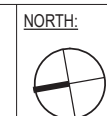


LOT NO:	DATE:	SCALE:	DRAWING No:	REV:
114	15-04-2026	1 : 100	CDC.11	3
DRAWN BY:	CHECKED BY:		ISSUED BY:	
AS	RH			
DRAFTED BY:	CLIENT NAME:			
SL	Abi Maharjan & Nikki Manandhar			

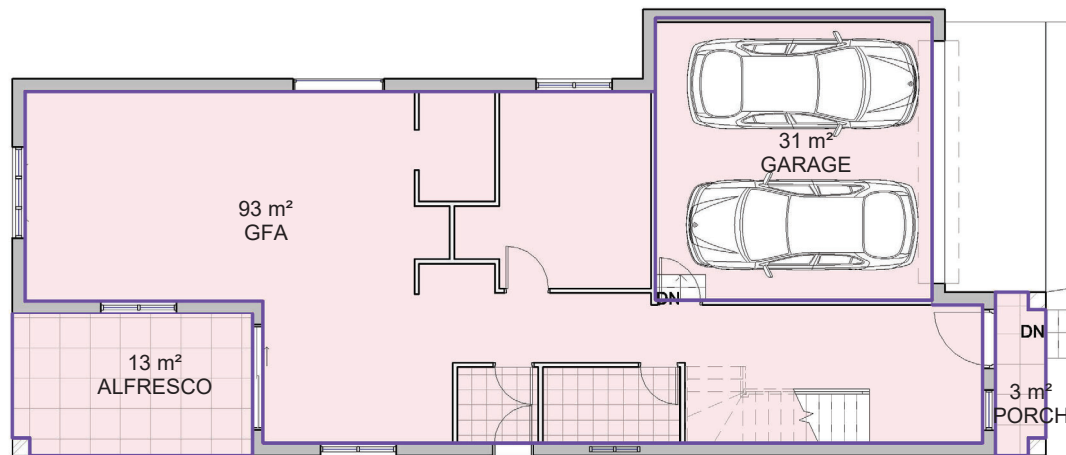

1 GROUND FLOOR
1 : 100

OnBuild Certifiers Pty Ltd Reference: 260016 Date: 16/04/2026	
Area Schedule (Rentable)	
Andrew Soliman Director/Principal Certifier BDC2940 Name	Area
Consultant who prepared this document remains responsible for accuracy	
ALFRESCO	13.43 m²
GFA	92.69 m²
GARAGE	30.69 m²
PORCH	3.04 m²
GROUND FLOOR: 4	139.84 m²

BALCONY	3.99 m²
FFA	87.69 m²
STAIR/VOID	8.07 m²
FIRST FLOOR: 3	99.75 m²
Grand total	239.59 m²

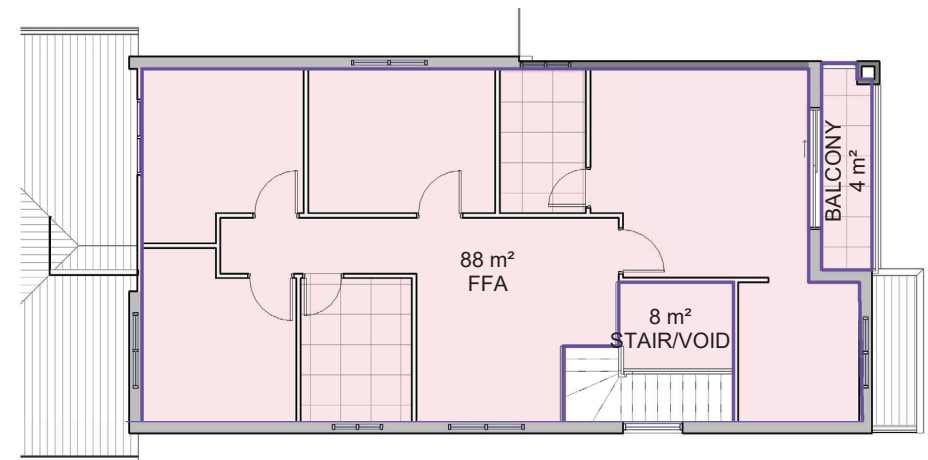

2 FIRST FLOOR
1 : 100

REV	DATE	DESCRIPTION	BY
3	3-02-2026	CDC ISSUE	
1	9-12-2025	Living & Alfresco extended to increase 5 sqm by Nava	

RUBY HOMES

THIS DRAWING IS THE EXCLUSIVE PROPERTY OF THE DEVELOPER & THE REPRODUCTION OF ANY PART WITHOUT THE PRIOR WRITTEN CONSENT OF THE DEVELOPER IS A VIOLATION OF APPLICABLE LAWS. IN NO EVENT SHALL THE DEVELOPER BE HELD LIABLE FOR SPECIAL, COLLATERAL, INCIDENTAL OR CONSEQUENTIAL LIABILITY IN CONNECTION WITH THE USE OF THIS DIGITAL DATA ONCE RELEASED FROM THE DEVELOPER'S OFFICE. THIS DRAWING IS TO BE READ & UNDERSTOOD IN CONJUNCTION WITH THE STRUCTURAL, MECHANICAL, ELECTRICAL & / OR ANY OTHER CONSULTANT'S DOCUMENTATION AS MAY BE APPLICABLE TO THE PROJECT PRIOR TO THE START OF ANY WORKS AND FOR ITS DURATION.

PROJECT:
LOT 114 47 TWELFTH AVENUE
47 TWELFTH AVENUE
AUSTRAL

DRAWING TITLE:
RENTABLE FLOOR
AREA PLAN



LOT NO:	DATE:	SCALE:	DRAWING No:	REV:
114	15-04-2026	1 : 100	CDC.12	3
DRAWN BY:	CHECKED BY:			ISSUED BY:
AS	RH			
DRAFTED BY:	CLIENT NAME:			
SL	Abi Maharjan & Nikki Manandhar			

OnBuild Certifiers Pty Ltd
Reference: 260016
Date: 16/04/2026
Andrew Soliman
Director/ Principal Certifier
BDC2940
Consultant who prepared this document
remains responsible for accuracy



	1. RF	2. BR1	3. CD1	4. CR1	5. AL	6. ED	7. GD	8. FAS	9. GUT
	ROOF	MAIN WALLS	CLADDING	ACCENT 1/RENDER	WINDOWS/ BALUSTRADE	MAIN DOOR	GARAGE DOOR	FASCIA	GUTTER
MATERIAL	COLORBOND	BRICK	BLUEBOARD	BRICK	ALUMINIUM	TIMBER	COLORBOND	COLORBOND	COLORBOND
COLOUR									

NOTE: ALL COLOURS SPECIFIED ARE INDICATIVE ONLY AND ARE SUBJECT TO VARIATION AND TO AVAILABILITY
ANY DISCREPANCY PLEASE FOLLOW AS PER RENDERED IMAGE

CDC ISSUE

REV	DATE	DESCRIPTION	BY
3	3-02-2026	CDC ISSUE	
1	9-12-2025	Living & Alfresco extended to increase 5 sqm by Nava	

RUBY HOMES


THIS DRAWING IS THE EXCLUSIVE PROPERTY OF THE DEVELOPER & THE REPRODUCTION OF ANY PART WITHOUT THE PRIOR WRITTEN CONSENT OF THE DEVELOPER IS A VIOLATION OF APPLICABLE LAWS. IN NO EVENT SHALL THE DEVELOPER BE HELD LIABLE FOR SPECIAL COLLATERAL, INCIDENTAL OR CONSEQUENTIAL LIABILITY IN CONNECTION WITH THE USE OF THIS DIGITAL DATA ONCE RELEASED FROM THE DEVELOPER'S OFFICE. THIS DRAWING IS TO BE READ & UNDERSTOOD IN CONJUNCTION WITH THE STRUCTURAL, MECHANICAL, ELECTRICAL & / OR ANY OTHER CONSULTANT'S DOCUMENTATION AS MAY BE APPLICABLE TO THE PROJECT PRIOR TO THE START OF ANY WORKS AND FOR ITS DURATION.

PROJECT:
LOT 114 47 TWELFTH AVENUE
47 TWELFTH AVENUE
AUSTRAL

DRAWING TITLE:
COLOR SCHEDULE



LOT NO:	DATE:	SCALE:	DRAWING No:	REV:
114	15-04-2026	1 : 100	CDC.14	3
DRAWN BY:	CHECKED BY:			ISSUED BY:
AS	RH			
DRAFTED BY:	CLIENT NAME:			
SL	Abi Maharjan & Nikki Manandhar			

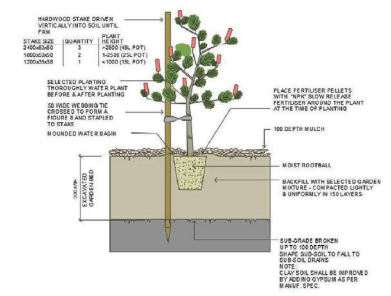[illegible]

2. TREE & SHRUB PLANTING IN GARDEN BED

NOTE :
DO NOT PLANT IN UNSUITABLE WEATHER CONDITIONS
SUCH AS EXTREME HEAT, COLD, WIND OR RAIN.
CLAY SOIL IS TO BE TREATED WITH CLAY BREAKER

AND ORGANIC COMPOST



RUBYS
HOMES

THIS DRAWING IS THE EXCLUSIVE PROPERTY OF THE DEVELOPER AND THE REPRODUCTION OF ANY PART WITHOUT THE PRIOR WRITTEN CONSENT OF THE DEVELOPER IS A VIOLATION OF APPLICABLE LAWS. IN NO EVENT SHALL THE DEVELOPER BE HELD LIABLE FOR SPECIAL, COLLATERAL, INCIDENTAL OR CONSEQUENTIAL LIABILITY IN CONNECTION WITH THE USE OF THIS DIGITAL DATA OR INFORMATION RELEASED FROM THE DEVELOPERS OFFICE. THIS DRAWING IS TO BE READ & UNDERSTOOD IN CONJUNCTION WITH THE STRUCTURAL, MECHANICAL, ELECTRICAL AND ALL OTHER CONSTRUCTION DOCUMENTATION AS MAY BE APPLICABLE TO THE PROJECT PRIOR TO THE START OF ANY WORKS

NORTH:



A3

ABCB HOUSING PROVISIONS : PART 10.2 WET AREA WATERPROOFING

10.2.1 Wet Areas

- Building elements in wet areas within a building must be protected with a waterproofing system.
- The waterproofing system in (1) must be either waterproof or water resistant in accordance with 10.2.2 to 10.2.6.

10.2.2 Shower Area (enclosed and unenclosed)

- For a shower area with a hob, step-down or level threshold, the following applies:
 - The floor of the **shower area** must be **waterproof**, including any hob or step-down (see Figure 10.2.2); and
 - The walls of the **shower area** must be **waterproof** not less than 1800 mm above the floor substrate (see Figure 10.2.2).
 - Wall junctions and joints within the **shower area** must be **waterproof** not less than 40 mm either side of the junction (see Figure 10.2.2).
 - Wall/floor junctions within the shower area must be **waterproof** (see Figure 10.2.2).
 - Penetrations within the **shower area** must be **waterproof**.
- A shower with a **preformed shower base** must also comply with the requirements of (1), except for (a) which is not applicable.

Figure 10.2.2: Extent of treatment for shower areas - concrete compressed fibre-cement and fibre-cement sheet floors.

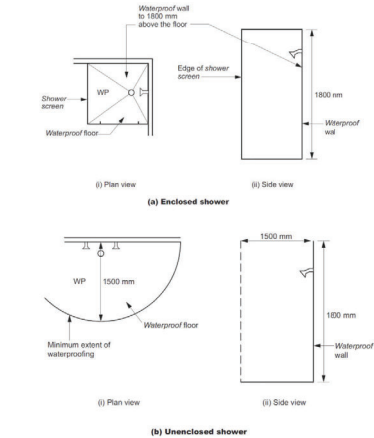


Figure Notes
 Wall/floor junction heights are to be as per 10.2.2 to 10.2.6 (as applicable).

Notes
 Where a shower is above a bath or spa, use requirements for shower.

10.2.3 Area outside shower area

- For concrete, compressed fibre-cement and fibre-cement sheet flooring, the floor of the room must be water resistant.
- For timber floors including particleboard, plywood and other timber based flooring materials, the floor of the room must be **waterproof**.
- Wall/floor junctions must be -
 - waterproof, and
 - where a flashing is used, the horizontal leg must be not less than 40 mm.

10.2.4 Areas adjacent to baths and spas without showers

- For areas adjacent to all baths and spas, the following applies:
 - For concrete, compressed fibre-cement and fibre-cement sheet flooring, the floor of the room must be water resistant.
 - For timber floors including particleboard, plywood and other timber based flooring materials, the floor of the room must be **waterproof**.
 - Tap and spout penetrations must be waterproof where they occur in horizontal surfaces.
- For areas adjacent to non-freestanding baths and spas, the following applies:
 - Walls must be water resistant (see Figure 10.2.4a and Figure 10.2.4b):
 - to a height of not less than 150mm above the vessel, for the extent of the vessel, where the vessel is within 75mm of a wall; and
 - for all exposed surfaces below vessel lip.
 - Wall junctions and joints must be water resistant within 150mm above a vessel for the extent of the vessel.
 - Wall/floor junctions must be waterproof for the extent of the vessel (see Figure 10.2.4a and Figure 10.2.4b).
- For inserted baths and spas, the following applies:
 - For floors and horizontal surfaces:
 - Any shelf area adjoining the bath or spa must be waterproof and include a waterstop under the vessel lip.
 - There are no requirements for the floor under a bath or spa.
 - For walls:
 - Waterproof to not less than 150mm above the lip of a bath or spa.
 - There are no requirements for the floor under a bath or spa.
 - For wall junctions and joints, the following applies:
 - Waterproof junctions within 150mm of a bath or spa.
 - There are no requirements for junctions and joints in walls beneath the lip of a bath or spa.
 - Tap and spout penetrations must be waterproof where they occur in horizontal surfaces.

Figure 10.2.4a: Areas adjacent to baths and spas without showers for concrete, compressed fibre-cement and fibre-cement sheet flooring




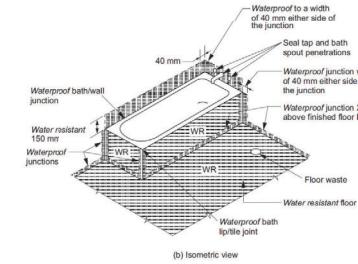



Figure 10.2.4b: Areas adjacent to baths and spas without showers for timber floors including particle-board, plywood and other floor materials

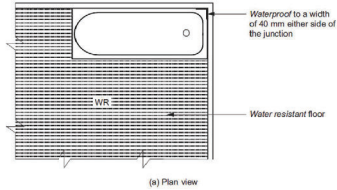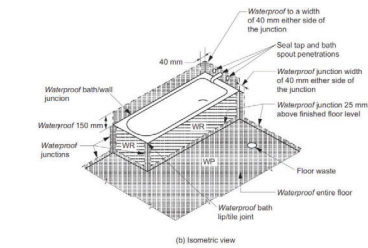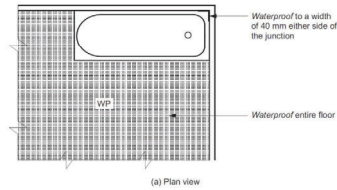

10.2.5 Other areas

- For walls adjoining other types of vessels (not tank, bath or laundry tub) the following applies:
 - Walls must be water resistant to a height of not less than 150mm above the vessel, for the extent of the vessel, where the vessel is within 75 mm of a wall (see Figure 10.2.5.)
 - Waterproof wall junctions where a vessel is fixed to a wall.
 - Waterproof tap and spout penetrations where they occur in surfaces required to be waterproof or water resistant.
- For laundries and WCs, the following applies:
 - The floor of the room must be waterproof.
 - Wall/floor junctions must be water resistant, and where a flashing is used, the horizontal leg must not be less than 40 mm.
- For WCs with handheld bidet spray installations, the following applies:
 - The floor of the room must be waterproof.
 - Walls must be -
 - Waterproof in WC area within a 900 mm radius from the wall connection of the handheld bidet spray device to a height of not less than 150mm above the floor substrate, and
 - water resistant in WC area within a 900 mm radius from the wall connection of the handheld bidet device to not less than 1200 mm above the finished floor level of the WC.
 - Wall junctions within the WC area within 900 mm radius from the wall connection of the handheld bidet spray device must be waterproof.
 - Wall/floor junctions within the WC area within 1000 mm radius from the wall connection of the handheld bidet spray device must be waterproof.
 - Penetrations in the WC area must be waterproof.

Figure 10.2.5: Bath and vessel abutting wall - areas to be protected

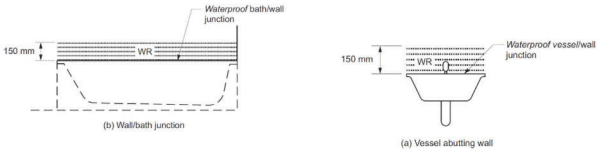

10.2.6 Waterproofing systems

- For the purposes of this Part, a waterproofing system is deemed -
 - waterproof, if it complies with (2); or
 - water resistant, if it complies with (3).
- For a waterproofing system required to be waterproof in accordance with 10.2.2 to 10.2.5, the materials nominated in 10.2.8 must be used.
- For a waterproofing system required to be water resistant in accordance with 10.2.2 to 10.2.5, the materials nominated in 10.2.9 must be used in conjunction with the materials in 10.2.10.

10.2.12 Construction of wet area floors - falls

Where a floor waste is installed -

- the minimum continuous fall of a floor plane to the waste must be 1:80; and
- the maximum continuous fall of a floor plane to the waste must be 1:50.

OnBuild Certifiers Pty Ltd
 Reference: 260016

Director/ Principal Certifier

BDC2940

I, the signatory, who prepared this document
 remains responsible for accuracy

3	3-02-2026	CDC ISSUE		
1	9-12-2025	Living & Alfresco extended to increase 5 sqm by Nava		
REV	DATE	DESCRIPTION		BY

PROJECT:
 LOT 114 47 TWELFTH AVENUE
 47 TWELFTH AVENUE
 AUSTRAL

DRAWING TITLE:
 WATERPROOFING DETAILS

NORTH:

LOT NO:
 114

DATE:
 15-04-2026

SCALE:
 1 : 50

DRAWING No:
 CDC.18

REV:
 3

ISSUED BY:
 Abi Maharjan & Nikki Manandhar