


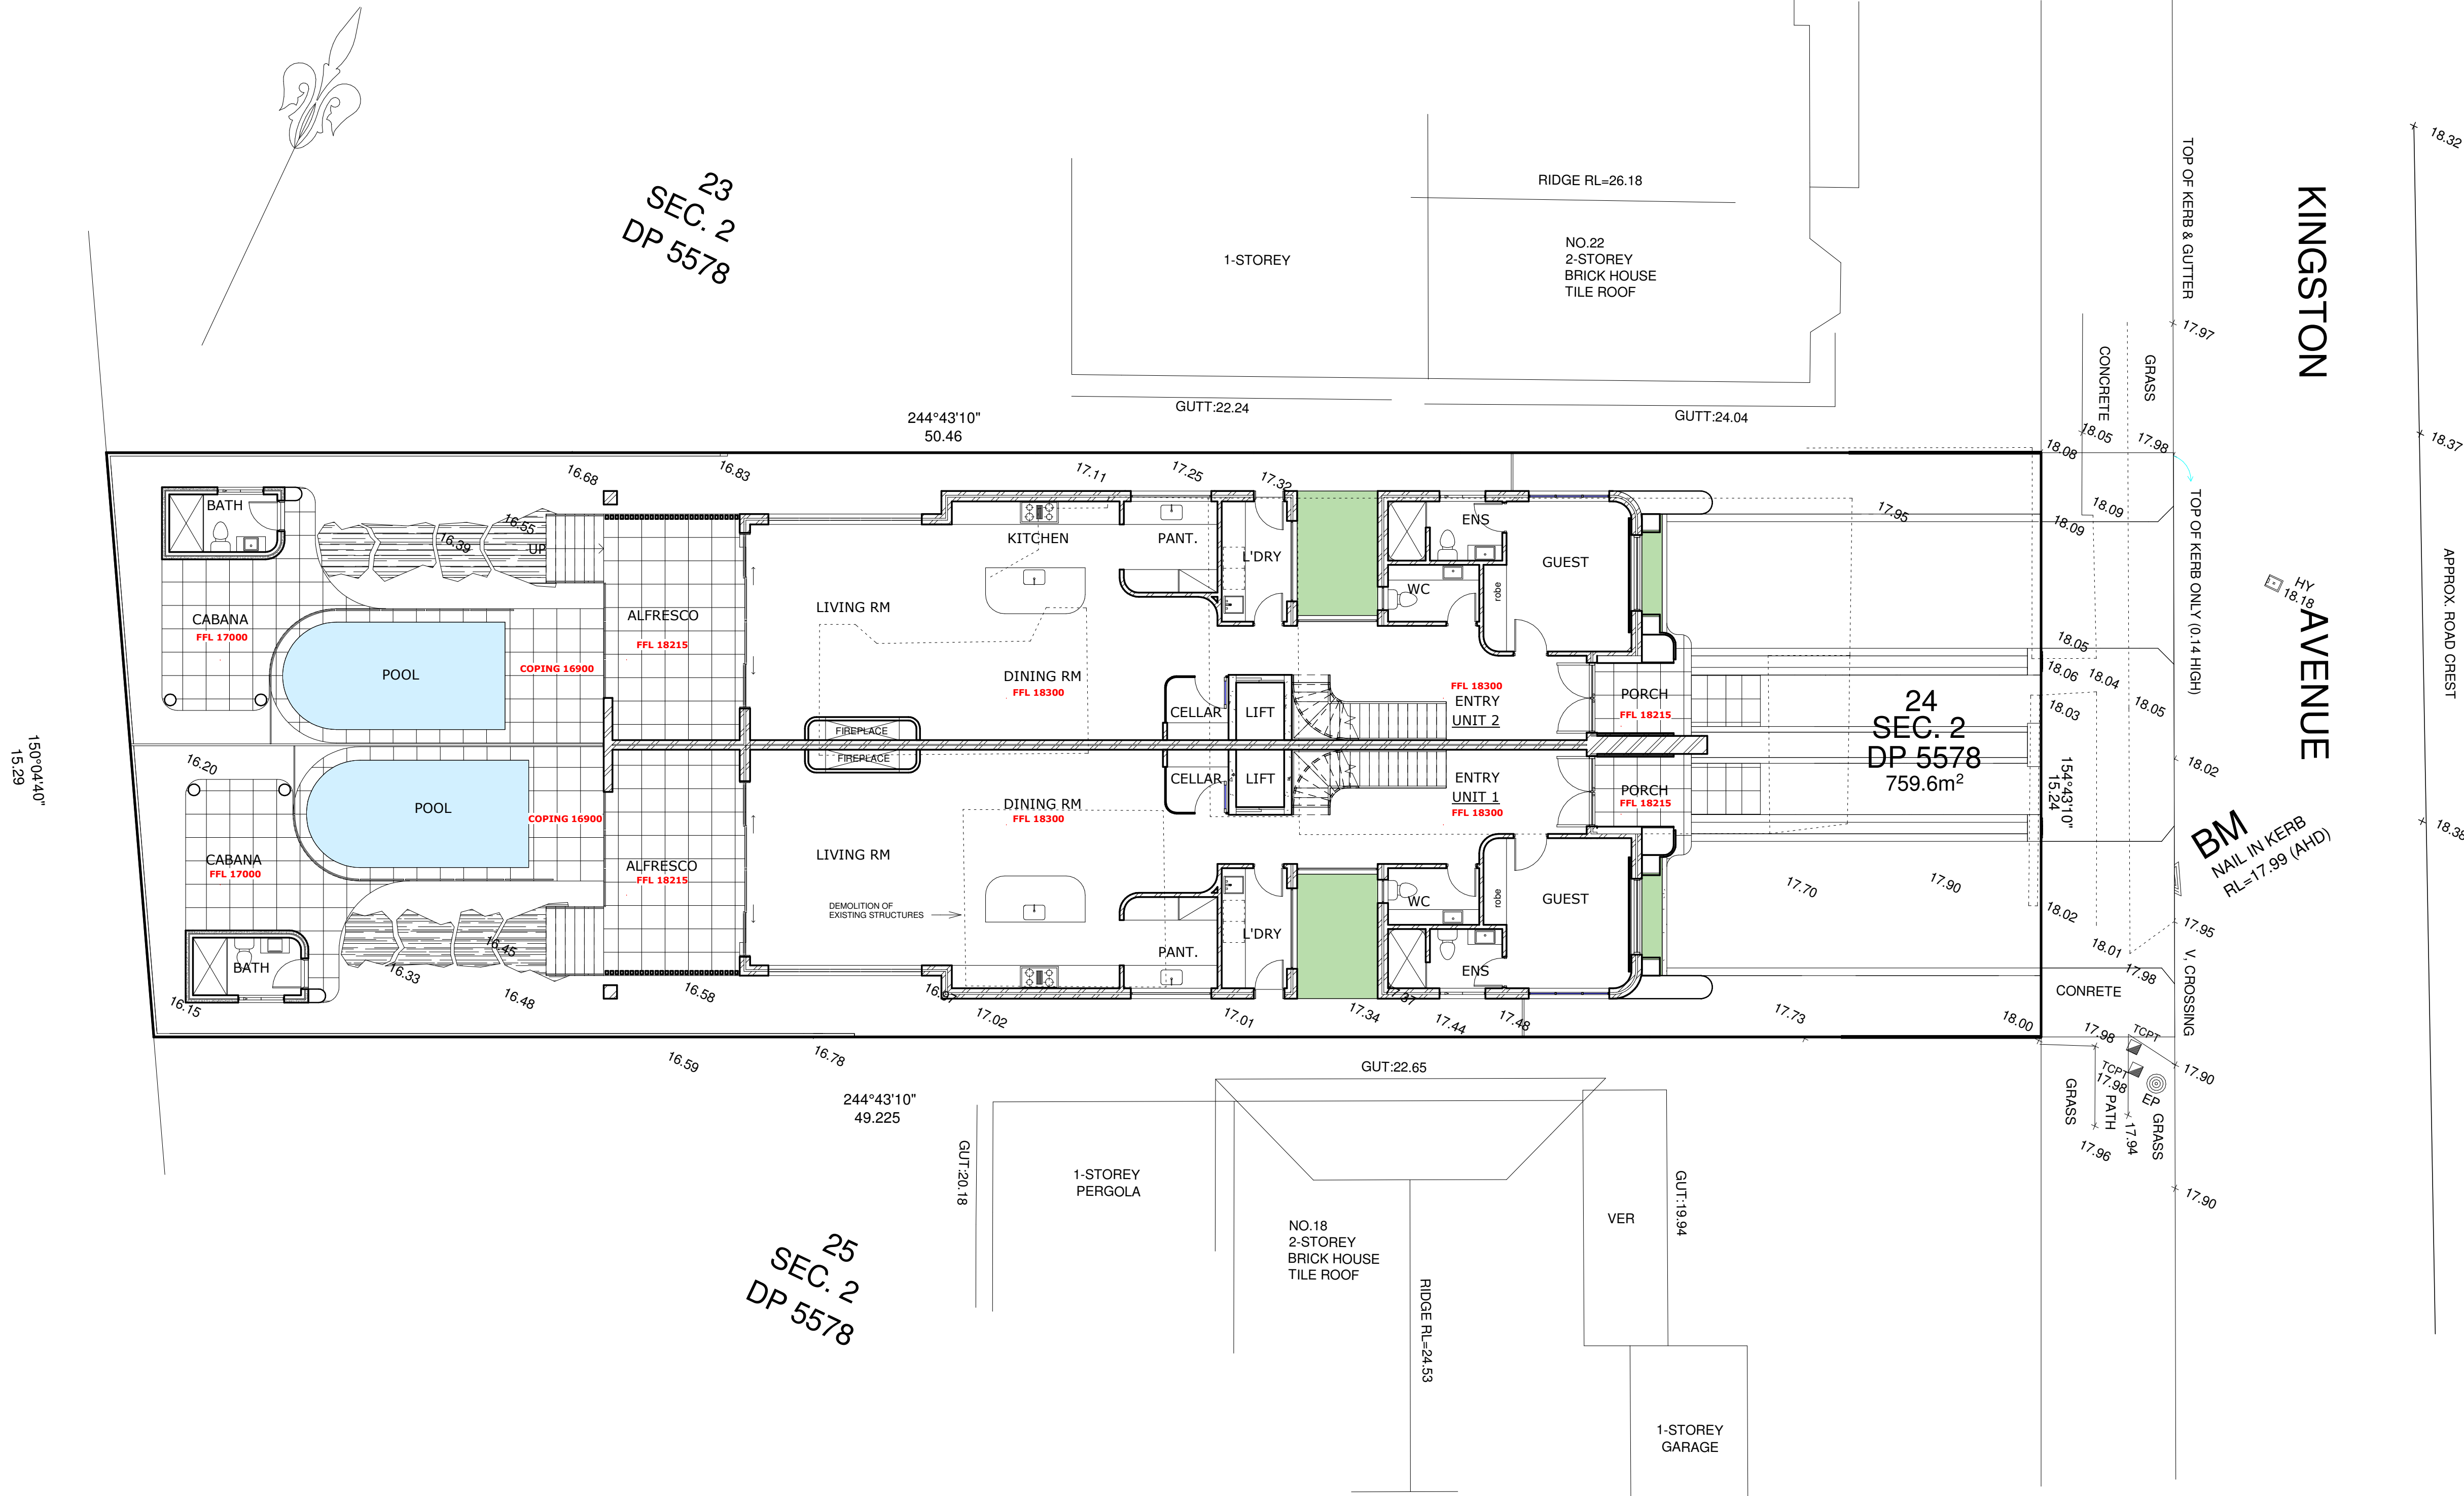

NOTES

1. ALL RUN OFF AND SEDIMENT CONTROL STRUCTURES WILL BE MAINTAINED IN A FUNCTIONAL CONDITION

2. REVEGETATION WORKS - HAY MULCHING MUST USE STRAW THAT IS GUARANTEED WEED FREE AND A "DRYLAND" SEED MIXTURE IN ALL APPLICATIONS

3. AREAS NOT USED FOR BUILDING SHOULD BE RETAINED WITH VEGETATION

4. REVEGETATION ON RETAIN CUT AND FILLS AS SOON AS POSSIBLE DURING CONSTRUCTION

TOPSOIL STOCKPILE
Covered with Poythene Membrane.

MATERIAL STORAGE AREA

DELIVERY TRUCK PARKING

WASTE BINS
12 cubic bin


KERB TURF FILTER

SEDIMENT FENCE

1

Site Plan

1 : 100

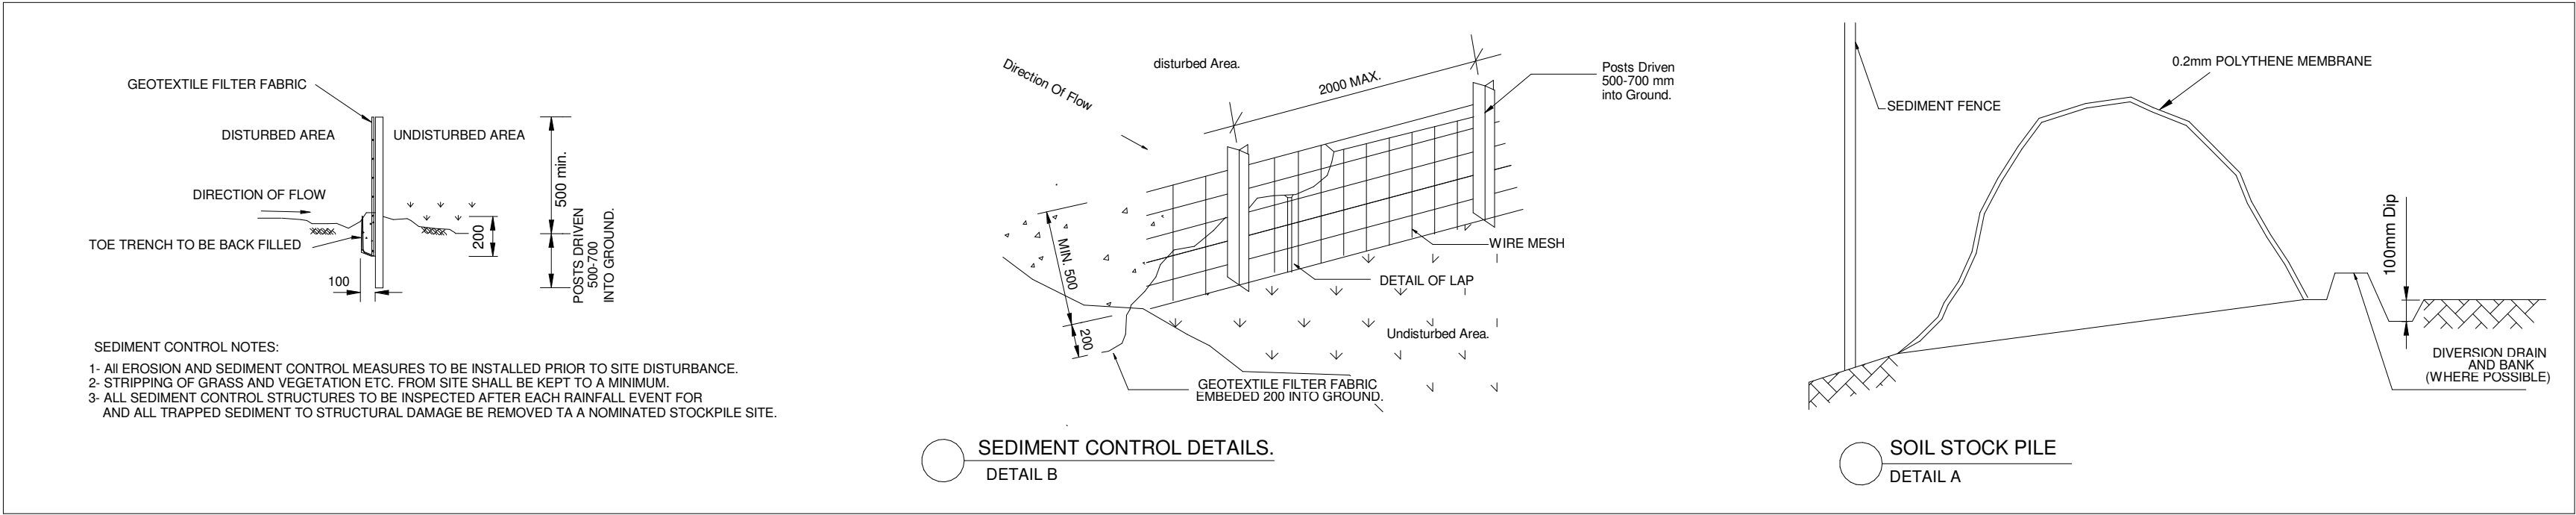

SHOP 1, 23-27 PATON STREET,
MERRYLANDS WEST, NSW 2160
(02) 9637 1111
jack@dvyne.com.au
www.dvyne.com.au
DESIGN | CONSTRUCT | CONSULT

JOB DESCRIPTION	DRAWING TITLE
Proposed duplex with Basement AT 20 Kingston Ave. Concord	SITE PLAN CLIENT DETAILS MANORBUILD p/I

DO NOT SCALE THE DRAWINGS. READ ALL DIMENSIONS SHOWN. ALL DIMENSIONS, NOTES ON ALL PLANS AND CONSENT DOCUMENTS MUST BE CHECKED AND VERIFIED BY THE CONTRACTOR PRIOR TO ANY COMMENCEMENT OF ANY BUILDING WORKS ON SITE, TO CLARIFY ANY DISCREPANCIES BETWEEN ALL PLAN DRAWINGS AND DOCUMENTATION RELEVANT TO THE PROPOSAL / SITE WORKS. GROUND LEVELS MAY VARY DUE TO SITE CONDITIONS. COPYRIGHT - THESE DRAWINGS REMAIN THE PROPERTY OF DVYNE DESIGN. JT PTY LTD AND CAN NOT BE ALTERED OR REPRODUCED WITHOUT WRITTEN CONSENT.	DRAWN	JT	ISSUE	AMENDMENT CONCEPT PLAN CDC SUBMISSION	BY	DATE
	DATE	DEC 2025				
	CHECKED	JACK				
	SCALE	1/100				
	JOB NUMBER	25251-00				
	NUMBER IN SET	A01				
	ISSUE	A	A		JT	NOV 2025
			B		JH	DEC 2025

1 Ground floor level

1 : 100



UNIT 1 WINDOW SCHEDULE

WINDOW WxH	WINDOW TYPE	HEAD HEIGHT
W1 2100 x 2500	ALUMINIUM FRAMED FIXED WINDOW - ARCHED HEAD	2700
W2 2100 x 600	ALUMINIUM FRAMED SLIDING WINDOW	2400
W3 1200 x 600	ALUMINIUM FRAMED SLIDING WINDOW OBSCURED	2400
W4 600 x 900	ALUMINIUM FRAMED AWNING WINDOW OBSCURED	2400
W5 2100 x 2700	ALUMINIUM FRAMED FIXED WINDOW	2700
W6 2100 x 2700	ALUMINIUM FRAMED FIXED WINDOW	2700
W7 2100 x 600	ALUMINIUM FRAMED FIXED WINDOW	1600
W8 4000 x 600	ALUMINIUM FRAMED SLIDING WINDOW	2400
W9 1200 x 600	ALUMINIUM FRAMED SLIDING WINDOW OBSCURED	2400
W10 1200 x 2400	ALUMINIUM FRAMED FIXED WINDOW - ARCHED HEAD	2400
W11 1000 x 2600	ALUMINIUM FRAMED FIXED WINDOW - PART CORNER WINDOW	2400
W12 2400 x 600	ALUMINIUM FRAMED SLIDING WINDOW	2400
W13 900 x 600	ALUMINIUM FRAMED SLIDING WINDOW OBSCURED	2400
W14 900 x 600	ALUMINIUM FRAMED SLIDING WINDOW OBSCURED	2400
W15 2400 x 600	ALUMINIUM FRAMED SLIDING WINDOW	2400
W16 1500 x 600	ALUMINIUM FRAMED SLIDING WINDOW OBSCURED	2400
W17 1500 x 1000	ALUMINIUM FRAMED SLIDING WINDOW	2400
W18 1500 x 1000	ALUMINIUM FRAMED SLIDING WINDOW	2400
W19 900 x 600	ALUMINIUM FRAMED AWNING WINDOW OBSCURED	2400
W20 2400 x 1000	ALUMINIUM FRAMED SLIDING WINDOW	2400

UNIT 1 DOOR SCHEDULE

DOOR WxH	DOOR TYPE	HEAD HEIGHT
SD1 4500 x 2400	ALUMINIUM FRAMED SLIDING DOOR	2400
SD2 3400 x 2400	ALUMINIUM FRAMED SLIDING DOOR	2600
D1 1890 x 2700	SELECTED ALUMINIUM ENTRY DOOR - TO BE MEASURED ON SITE	2700
D2 820 x 2340	SELECTED TIMBER FRAME SWING DOOR	2400
D3 720 x 2340	SELECTED TIMBER FRAME SWING DOOR	2400
D4 720 x 2340	SELECTED TIMBER FRAME EXTERNAL SWING DOOR	2400
GD 2600 x 2400	SELECTED PANEL LIFT GARAGE DOOR	2400

UNIT 2 WINDOW SCHEDULE

WINDOW WxH	WINDOW TYPE	HEAD HEIGHT
W1A 2100 x 2500	ALUMINIUM FRAMED FIXED WINDOW - ARCHED HEAD	2700
W2A 2100 x 600	ALUMINIUM FRAMED SLIDING WINDOW	2400
W3A 1200 x 600	ALUMINIUM FRAMED SLIDING WINDOW OBSCURED	2400
W4A 600 x 900	ALUMINIUM FRAMED AWNING WINDOW OBSCURED	2400
W5A 2100 x 2700	ALUMINIUM FRAMED FIXED WINDOW	2700
W6A 2100 x 2700	ALUMINIUM FRAMED FIXED WINDOW	2700
W7A 2100 x 600	ALUMINIUM FRAMED FIXED WINDOW	1600
W8A 4000 x 600	ALUMINIUM FRAMED SLIDING WINDOW	2400
W9A 1200 x 600	ALUMINIUM FRAMED SLIDING WINDOW OBSCURED	2400
W10A 1200 x 2400	ALUMINIUM FRAMED FIXED WINDOW - ARCHED HEAD	2400
W11A 1000 x 2600	ALUMINIUM FRAMED FIXED WINDOW - PART CORNER WINDOW	2400
W12A 2400 x 600	ALUMINIUM FRAMED SLIDING WINDOW	2400
W13A 900 x 600	ALUMINIUM FRAMED SLIDING WINDOW OBSCURED	2400
W14A 900 x 600	ALUMINIUM FRAMED SLIDING WINDOW OBSCURED	2400
W15A 2400 x 600	ALUMINIUM FRAMED SLIDING WINDOW	2400
W16A 1500 x 600	ALUMINIUM FRAMED SLIDING WINDOW OBSCURED	2400
W17A 1500 x 1000	ALUMINIUM FRAMED SLIDING WINDOW	2400
W18A 1500 x 1000	ALUMINIUM FRAMED SLIDING WINDOW	2400
W19A 900 x 600	ALUMINIUM FRAMED AWNING WINDOW OBSCURED	2400
W20A 2400 x 1000	ALUMINIUM FRAMED SLIDING WINDOW	2400

UNIT 2 DOOR SCHEDULE

DOOR WxH	DOOR TYPE	HEAD HEIGHT
SD1A 4500 x 2400	ALUMINIUM FRAMED SLIDING DOOR	2400
SD2A 3400 x 2400	ALUMINIUM FRAMED SLIDING DOOR	2600
D1 1890 x 2700	SELECTED ALUMINIUM ENTRY DOOR - TO BE MEASURED ON SITE	2700
D2 820 x 2340	SELECTED TIMBER FRAME SWING DOOR	2400
D3 720 x 2340	SELECTED TIMBER FRAME SWING DOOR	2400
D4 720 x 2340	SELECTED TIMBER FRAME EXTERNAL SWING DOOR	2400
GD 2600 x 2400	SELECTED PANEL LIFT GARAGE DOOR	2400

LEGEND

- SMOKE ALARM CLAUSE 9.5.4 OF HOUSING PROVISIONS 2022
- FLOOR WASTE
- MECHANICAL VENTILATION CLAUSE 10.6.2 OF HOUSING PROVISIONS 2022
- LOCATION OF HOT WATER SYSTEM AS PER BASIX REQUIREMENTS
- LOCATION OF AIR CONDITIONING UNIT AS PER BASIX REQUIREMENTS



SHOP 1, 23-27 PATON STREET,
MERRYLANDS WEST, NSW 2160
(02) 9637 1111
jack@dvyne.com.au
www.dvyne.com.au
DESIGN | CONSTRUCT | CONSULT

JOB DESCRIPTION
Proposed duplex with Basement
AT
20 Kingston Ave. Concord

DRAWING TITLE
FLOOR PLANS
CLIENT DETAILS
MANORBUILD p/I


DO NOT SCALE THE DRAWINGS. READ ALL DIMENSIONS SHOWN.
ALL DIMENSIONS, NOTES ON ALL PLANS AND CONSENT
DOCUMENTS MUST BE CHECKED AND VERIFIED BY THE
CONTRACTOR PRIOR TO ANY COMMENCEMENT OF ANY
BUILDING WORKS ON SITE, TO CLARIFY ANY DISCREPANCIES
BETWEEN ALL PLAN DRAWINGS AND DOCUMENTATION RELEVANT TO THE
PROPOSAL / SITE WORKS. GROUND LEVELS MAY VARY DUE TO SITE
CONDITIONS. COPYRIGHT - THESE DRAWINGS REMAIN THE PROPERTY OF
Dvyne Design JT PTY LTD AND CAN NOT BE ALTERED OR REPRODUCED
WITHOUT WRITTEN CONSENT.

DRAWN JT
DATE NOV 2025
CHECKED JACK
SCALE 1:100
JOB NUMBER 25251-00
NUMBER IN SET A02
ISSUE A

ISSUE
A
B

AMENDMENT
CONCEPT PLAN
CDC SUBMISSION

BY JT
DATE NOV 2025
JH DEC 2025

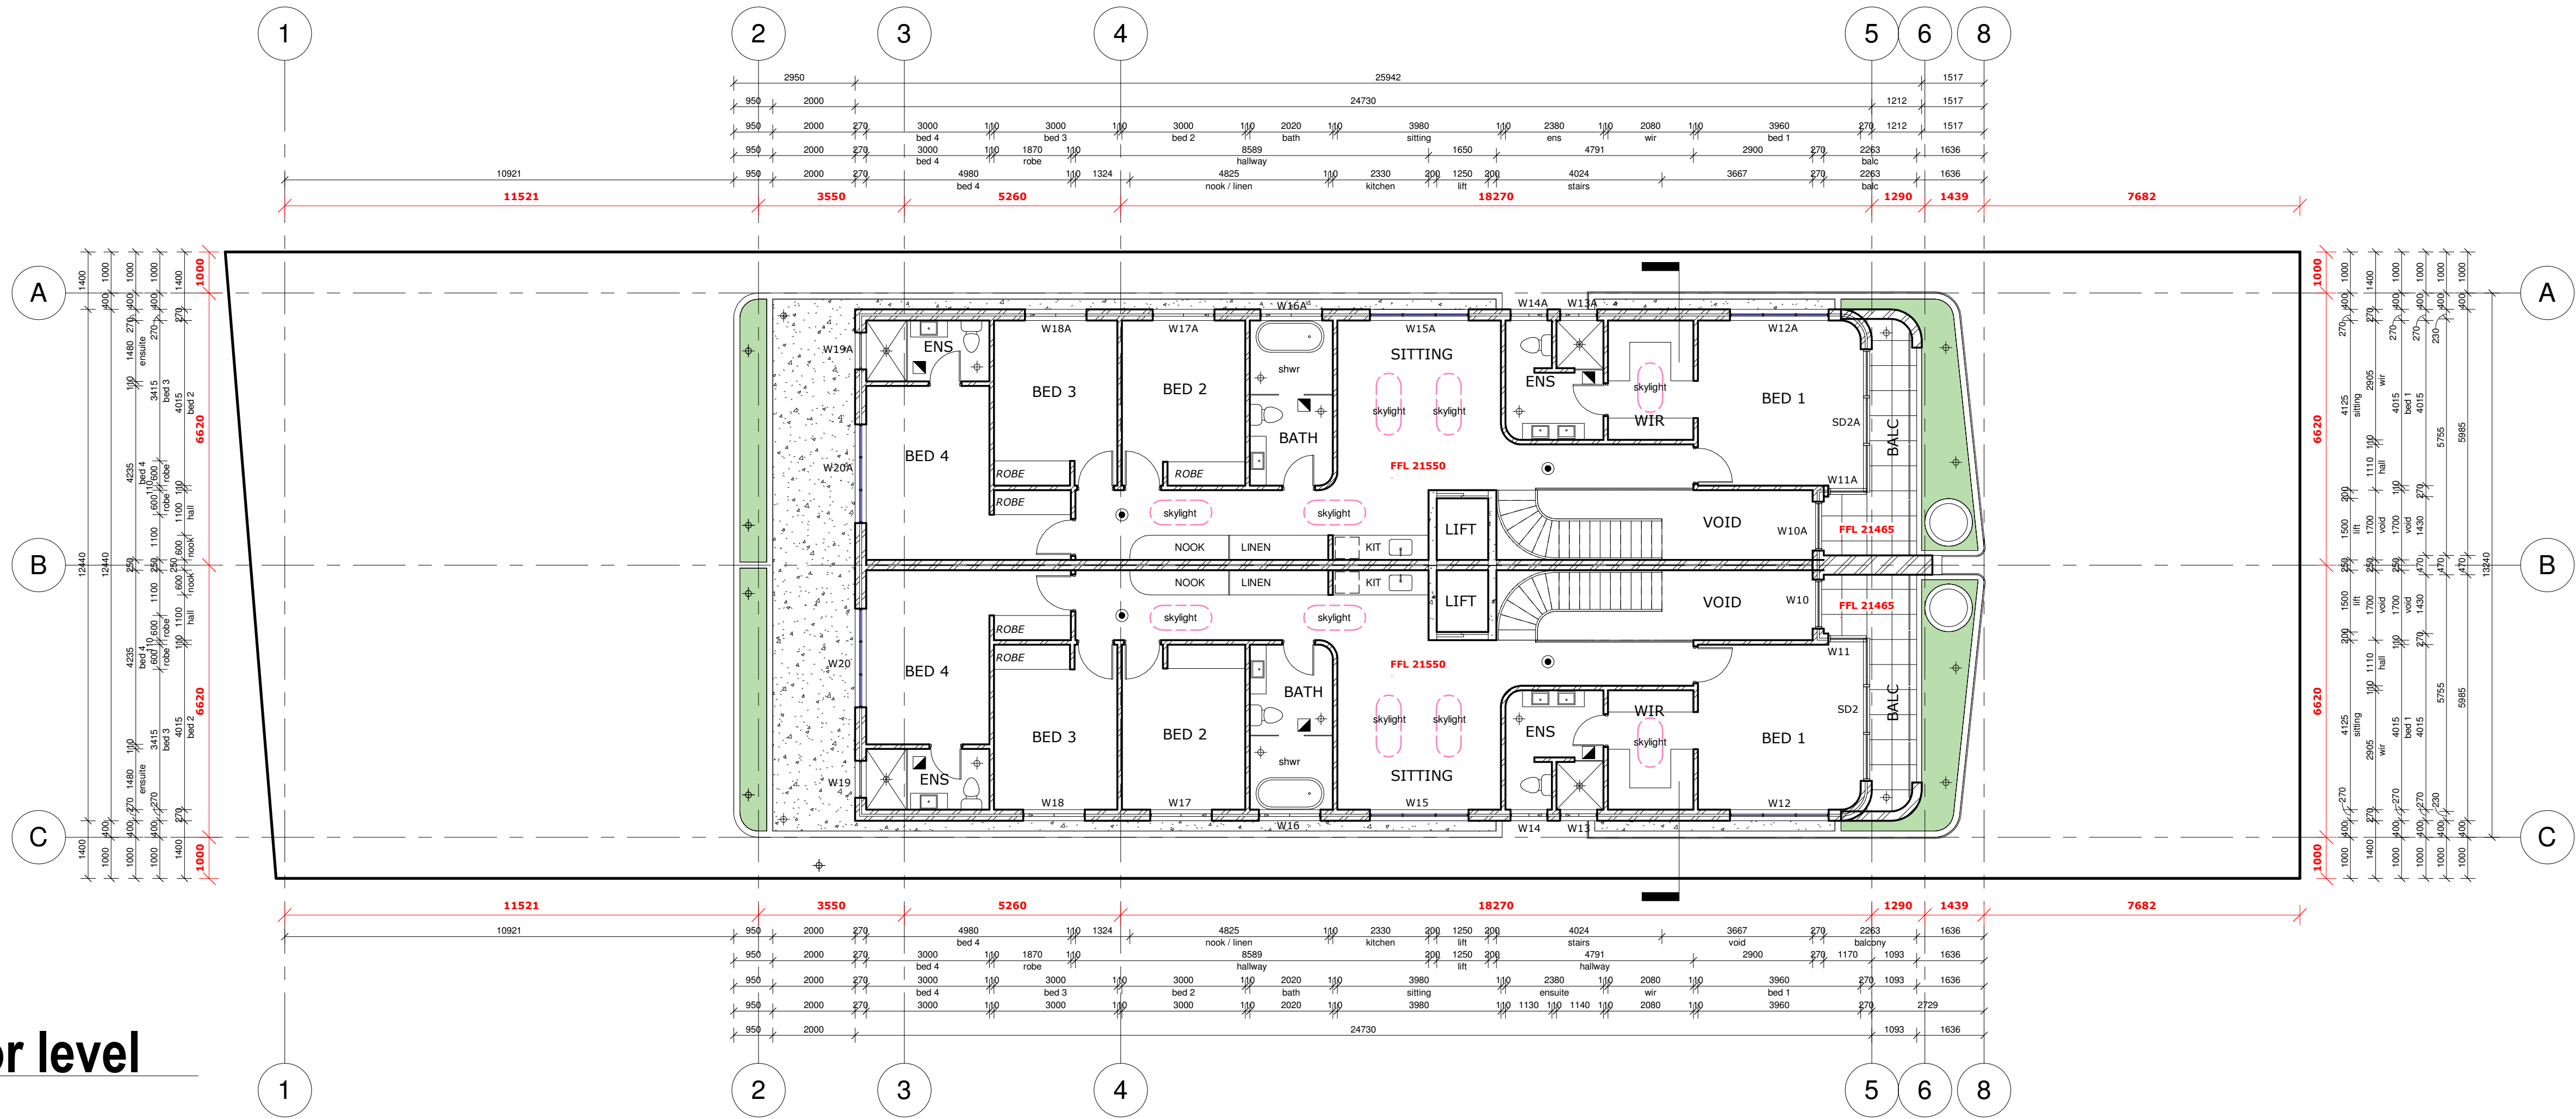

1 First floor level
1:100

UNIT 1 WINDOW SCHEDULE

WINDOW WxH	WINDOW TYPE	HEAD HEIGHT
W1 2100 x 2500	ALUMINIUM FRAMED FIXED WINDOW - ARCHED HEAD	2700
W2 2100 x 600	ALUMINIUM FRAMED SLIDING WINDOW	2400
W3 1200 x 600	ALUMINIUM FRAMED SLIDING WINDOW OBSCURED	2400
W4 600 x 900	ALUMINIUM FRAMED AWNING WINDOW OBSCURED	2400
W5 2100 x 2700	ALUMINIUM FRAMED FIXED WINDOW	2700
W6 2100 x 2700	ALUMINIUM FRAMED FIXED WINDOW	2700
W7 2100 x 600	ALUMINIUM FRAMED FIXED WINDOW	1600
W8 4000 x 600	ALUMINIUM FRAMED SLIDING WINDOW	2400
W9 1200 x 600	ALUMINIUM FRAMED SLIDING WINDOW OBSCURED	2400
W10 1200 x 2400	ALUMINIUM FRAMED FIXED WINDOW - ARCHED HEAD	2400
W11 1000 x 2600	ALUMINIUM FRAMED FIXED WINDOW - PART CORNER WINDOW	2400
W12 2400 x 600	ALUMINIUM FRAMED SLIDING WINDOW	2400
W13 900 x 600	ALUMINIUM FRAMED SLIDING WINDOW OBSCURED	2400
W14 900 x 600	ALUMINIUM FRAMED SLIDING WINDOW OBSCURED	2400
W15 2400 x 600	ALUMINIUM FRAMED SLIDING WINDOW	2400
W16 1500 x 600	ALUMINIUM FRAMED SLIDING WINDOW OBSCURED	2400
W17 1500 x 1000	ALUMINIUM FRAMED SLIDING WINDOW	2400
W18 1500 x 1000	ALUMINIUM FRAMED SLIDING WINDOW	2400
W19 900 x 600	ALUMINIUM FRAMED AWNING WINDOW OBSCURED	2400
W20 2400 x 1000	ALUMINIUM FRAMED SLIDING WINDOW	2400

UNIT 1 DOOR SCHEDULE

DOOR WxH	DOOR TYPE	HEAD HEIGHT
SD1 4500 x 2400	ALUMINIUM FRAMED SLIDING DOOR	2400
SD2 3400 x 2400	ALUMINIUM FRAMED SLIDING DOOR	2600
D1 1890 x 2700	SELECTED ALUMINIUM ENTRY DOOR - TO BE MEASURED ON SITE	2700
D2 820 x 2340	SELECTED TIMBER FRAME SWING DOOR	2400
D3 720 x 2340	SELECTED TIMBER FRAME SWING DOOR	2400
D4 720 x 2340	SELECTED TIMBER FRAME EXTERNAL SWING DOOR	2400
GD 2600 x 2400	SELECTED PANEL LIFT GARAGE DOOR	2400

UNIT 2 WINDOW SCHEDULE

WINDOW WxH	WINDOW TYPE	HEAD HEIGHT
W1A 2100 x 2500	ALUMINIUM FRAMED FIXED WINDOW - ARCHED HEAD	2700
W2A 2100 x 600	ALUMINIUM FRAMED SLIDING WINDOW	2400
W3A 1200 x 600	ALUMINIUM FRAMED SLIDING WINDOW OBSCURED	2400
W4A 600 x 900	ALUMINIUM FRAMED AWNING WINDOW OBSCURED	2400
W5A 2100 x 2700	ALUMINIUM FRAMED FIXED WINDOW	2700
W6A 2100 x 2700	ALUMINIUM FRAMED FIXED WINDOW	2700
W7A 2100 x 600	ALUMINIUM FRAMED FIXED WINDOW	1600
W8A 4000 x 600	ALUMINIUM FRAMED SLIDING WINDOW	2400
W9A 1200 x 600	ALUMINIUM FRAMED SLIDING WINDOW OBSCURED	2400
W10A 1200 x 2400	ALUMINIUM FRAMED FIXED WINDOW - ARCHED HEAD	2400
W11A 1000 x 2600	ALUMINIUM FRAMED FIXED WINDOW - PART CORNER WINDOW	2400
W12A 2400 x 600	ALUMINIUM FRAMED SLIDING WINDOW	2400
W13A 900 x 600	ALUMINIUM FRAMED SLIDING WINDOW OBSCURED	2400
W14A 900 x 600	ALUMINIUM FRAMED SLIDING WINDOW OBSCURED	2400
W15A 2400 x 600	ALUMINIUM FRAMED SLIDING WINDOW	2400
W16A 1500 x 600	ALUMINIUM FRAMED SLIDING WINDOW OBSCURED	2400
W17A 1500 x 1000	ALUMINIUM FRAMED SLIDING WINDOW	2400
W18A 1500 x 1000	ALUMINIUM FRAMED SLIDING WINDOW	2400
W19A 900 x 600	ALUMINIUM FRAMED AWNING WINDOW OBSCURED	2400
W20A 2400 x 1000	ALUMINIUM FRAMED SLIDING WINDOW	2400

UNIT 2 DOOR SCHEDULE

DOOR WxH	DOOR TYPE	HEAD HEIGHT
SD1A 4500 x 2400	ALUMINIUM FRAMED SLIDING DOOR	2400
SD2A 3400 x 2400	ALUMINIUM FRAMED SLIDING DOOR	2600
D1 1890 x 2700	SELECTED ALUMINIUM ENTRY DOOR - TO BE MEASURED ON SITE	2700
D2 820 x 2340	SELECTED TIMBER FRAME SWING DOOR	2400
D3 720 x 2340	SELECTED TIMBER FRAME SWING DOOR	2400
D4 720 x 2340	SELECTED TIMBER FRAME EXTERNAL SWING DOOR	2400
GD 2600 x 2400	SELECTED PANEL LIFT GARAGE DOOR	2400

LEGEND	
	SMOKE ALARM CLAUSE 9.5.4 OF HOUSING PROVISIONS 2022
	FLOOR WASTE
	MECHANICAL VENTILATION CLAUSE 10.6.2 OF HOUSING PROVISIONS 2022
	LOCATION OF HOT WATER SYSTEM AS PER BASIX REQUIREMENTS
	LOCATION OF AIR CONDITIONING UNIT AS PER BASIX REQUIREMENTS



SHOP 1, 23-27 PATON STREET,
MERRYLANDS WEST, NSW 2160
(02) 9637 1111
jack@dvyne.com.au
www.dvyne.com.au
DESIGN | CONSTRUCT | CONSULT

JOB DESCRIPTION
Proposed duplex with Basement
AT
20 Kingston Ave. Concord

DRAWING TITLE
FIRST FLOOR
CLIENT DETAILS
MANORBUILD p/I



DO NOT SCALE THE DRAWINGS. READ ALL DIMENSIONS SHOWN.
ALL DIMENSIONS, NOTES ON ALL PLANS AND CONSENT
DOCUMENTS MUST BE CHECKED AND VERIFIED BY THE
CONTRACTOR PRIOR TO ANY COMMENCEMENT OF ANY
BUILDING WORKS ON SITE, TO CLARIFY ANY DISCREPANCIES
BETWEEN ALL PLAN DRAWINGS AND DOCUMENTATION RELEVANT TO THE
PROPOSAL / SITE WORKS. GROUND LEVELS MAY VARY DUE TO SITE
CONDITIONS. COPYRIGHT - THESE DRAWINGS REMAIN THE PROPERTY OF
Dvyne DESIGN JT PTY LTD AND CAN NOT BE ALTERED OR REPRODUCED
WITHOUT WRITTEN CONSENT.

DRAWN JT
DATE DEC 2025
CHECKED JACK
SCALE 1:100
JOB NUMBER 25251-00
NUMBER IN SET A03
ISSUE A


ISSUE
A
B

AMENDMENT
CONCEPT PLAN
CDC SUBMISSION


BY JT
DATE NOV 2025
JH DEC 2025

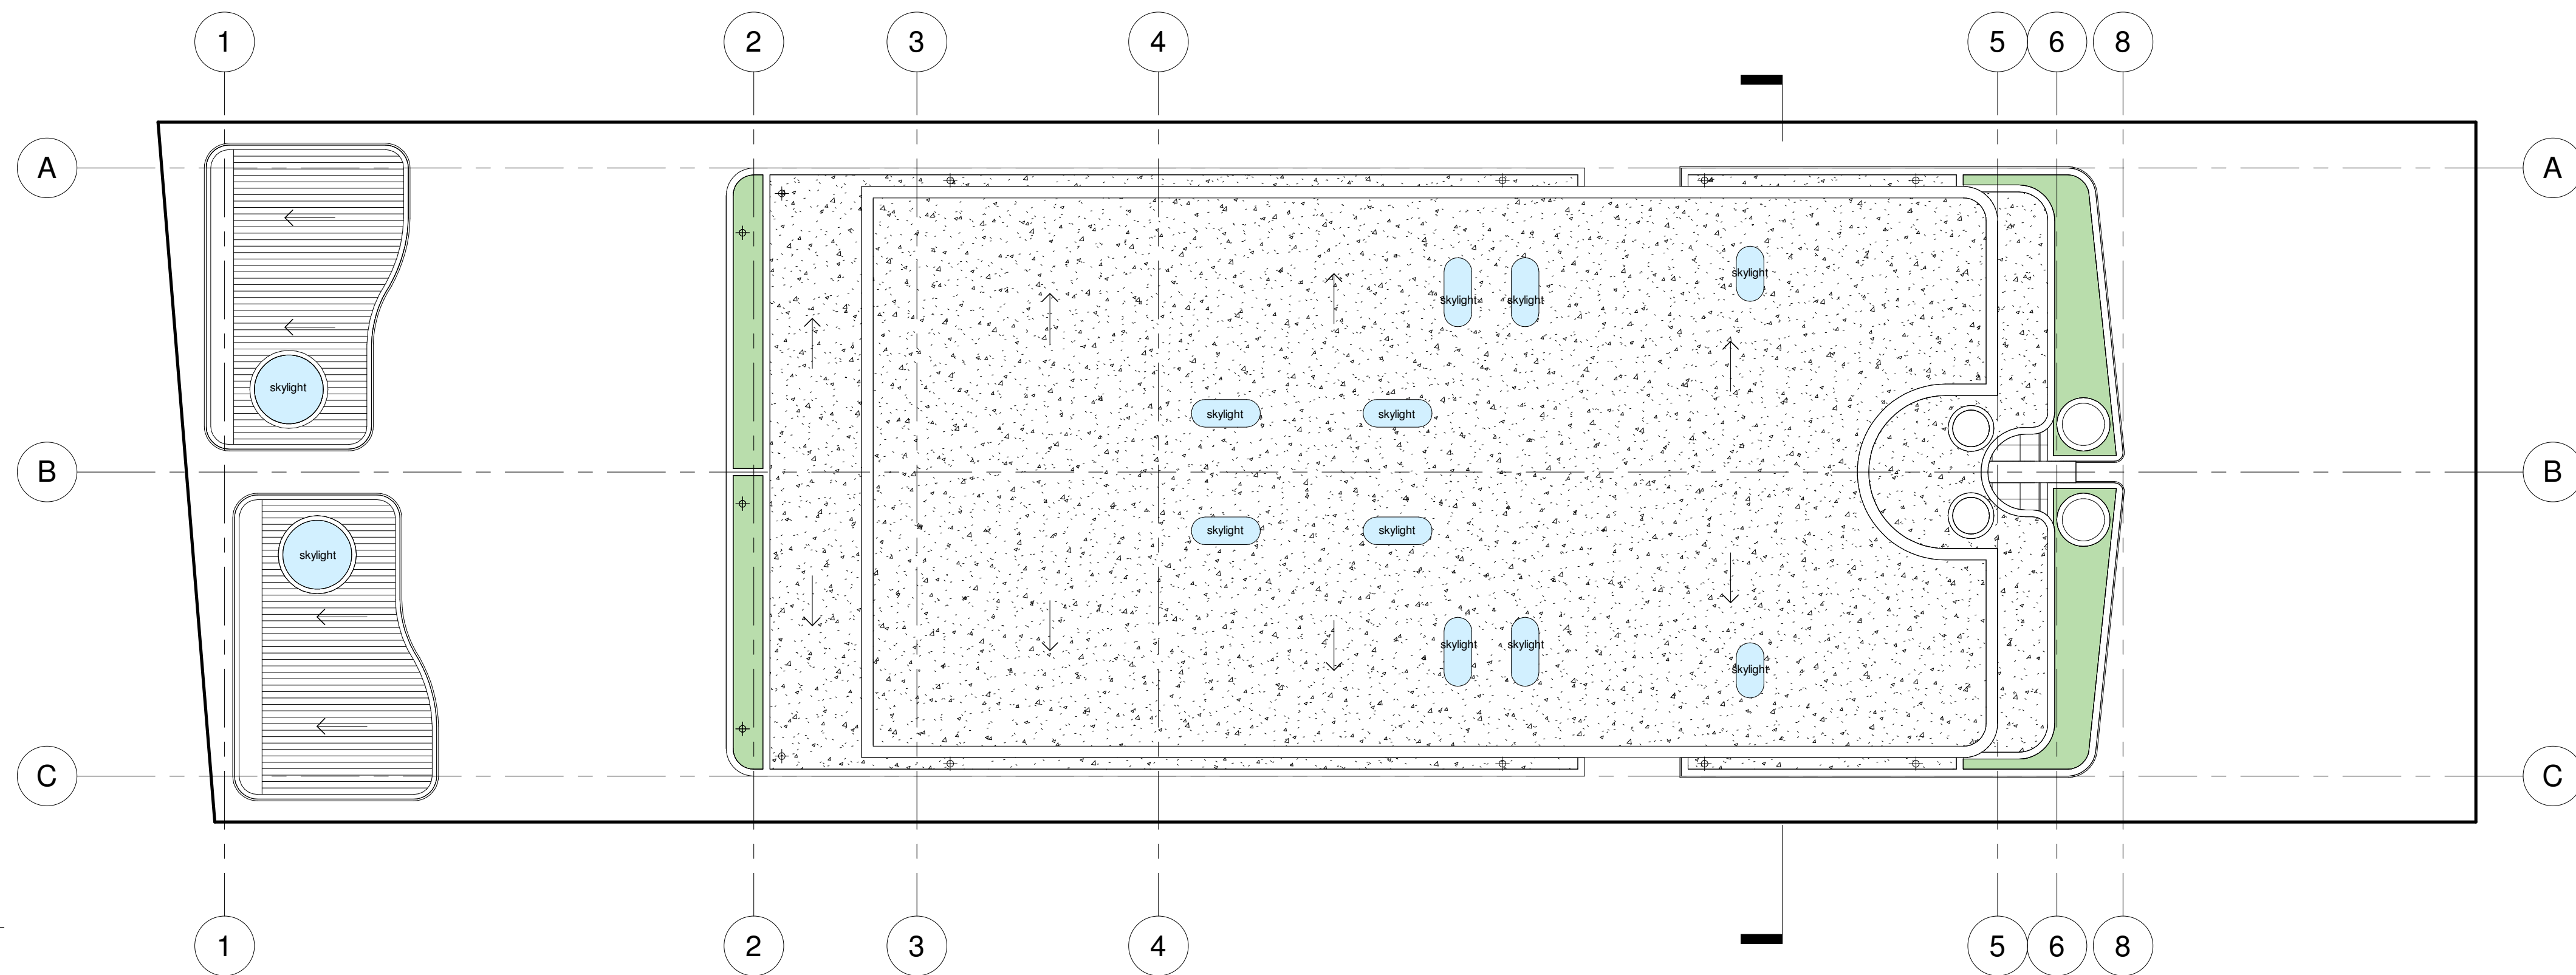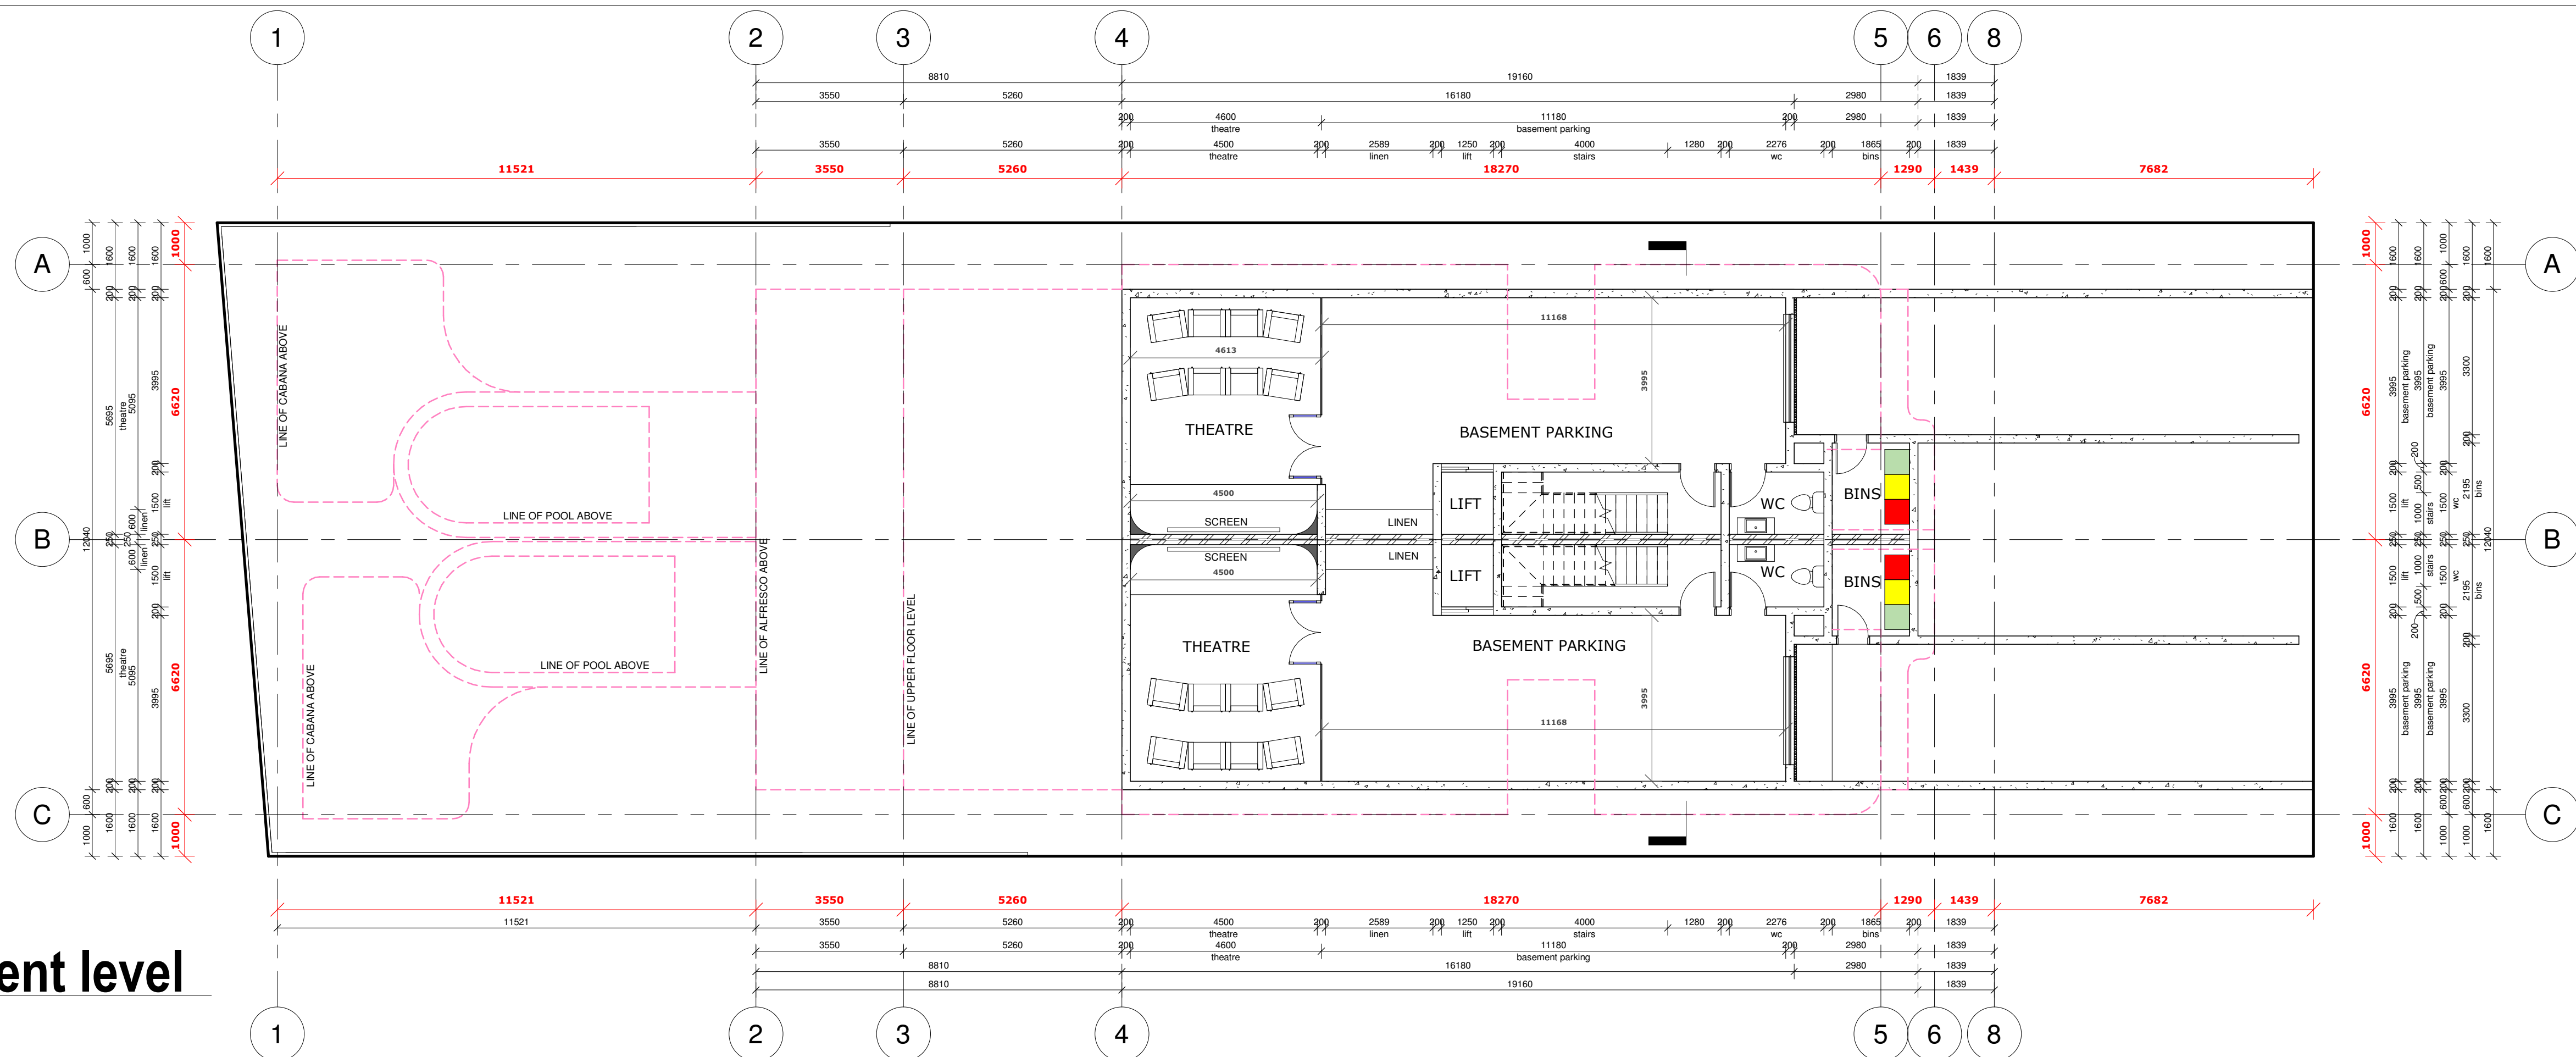


Protection of Operable Windows
Clause 11.3.7 of the Housing Provisions 2022
Balustrades Installation Clause 11.3.4
of the Housing Provisions 2022

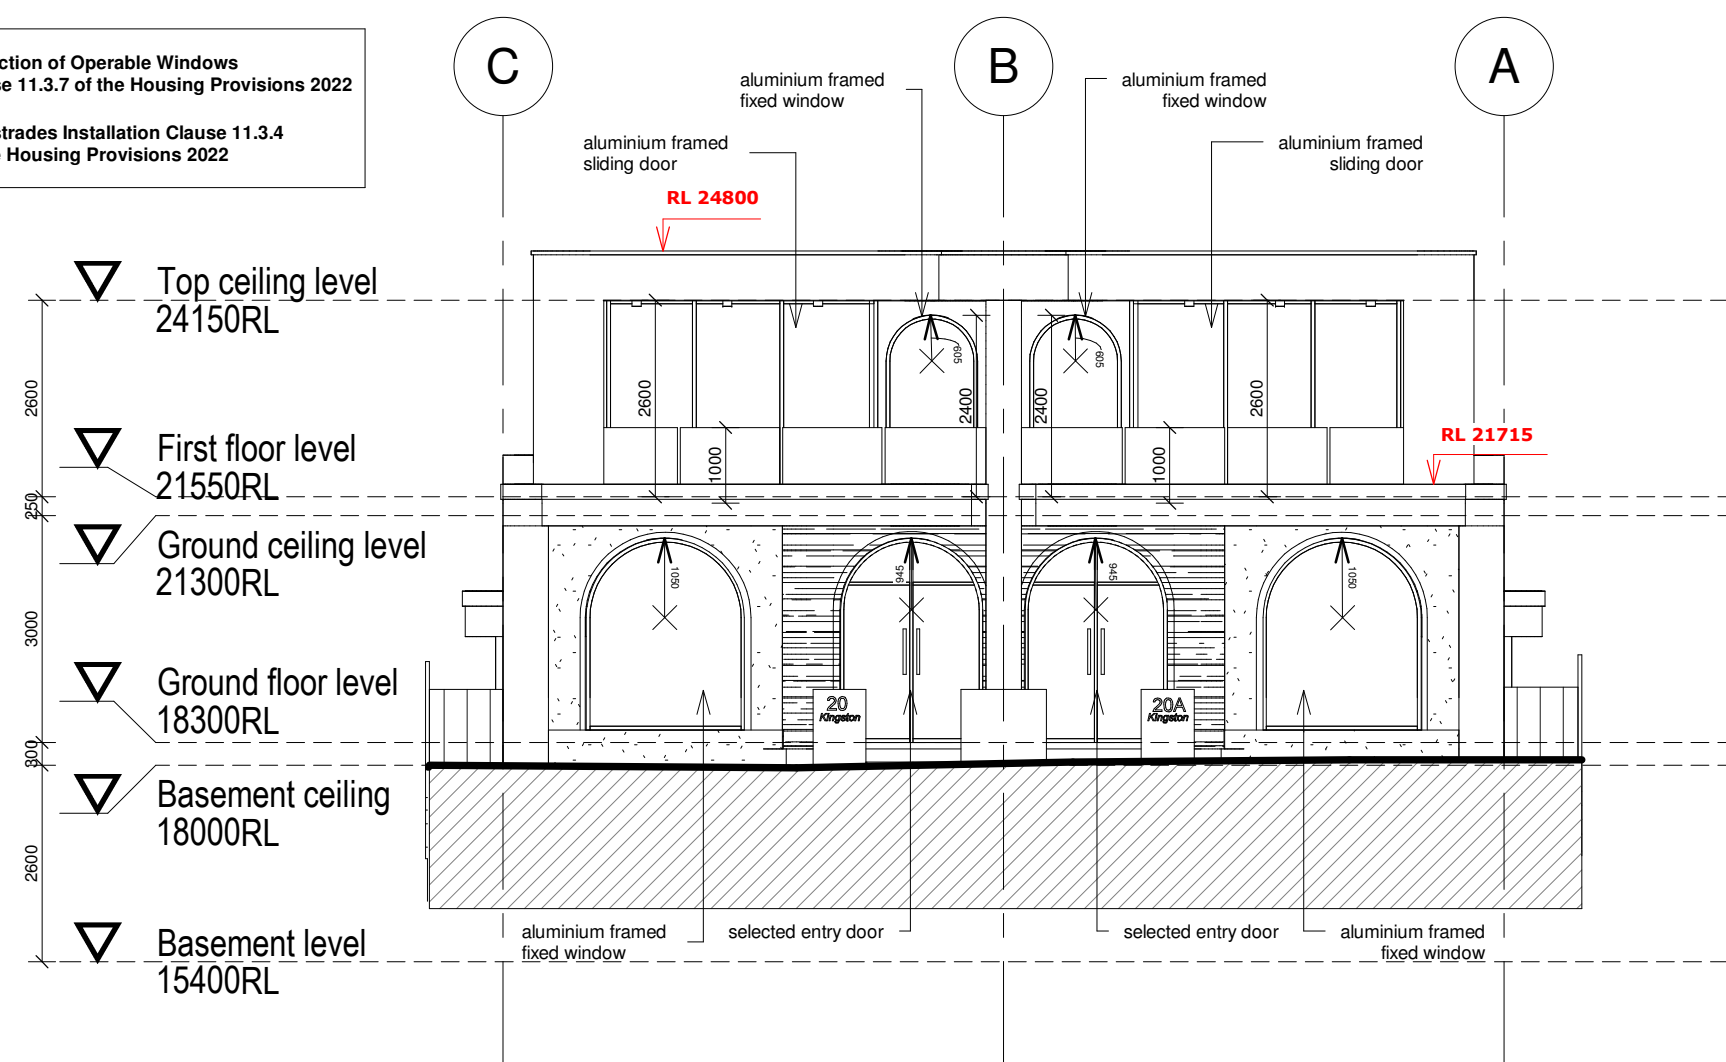

1 East elevation
1 : 100

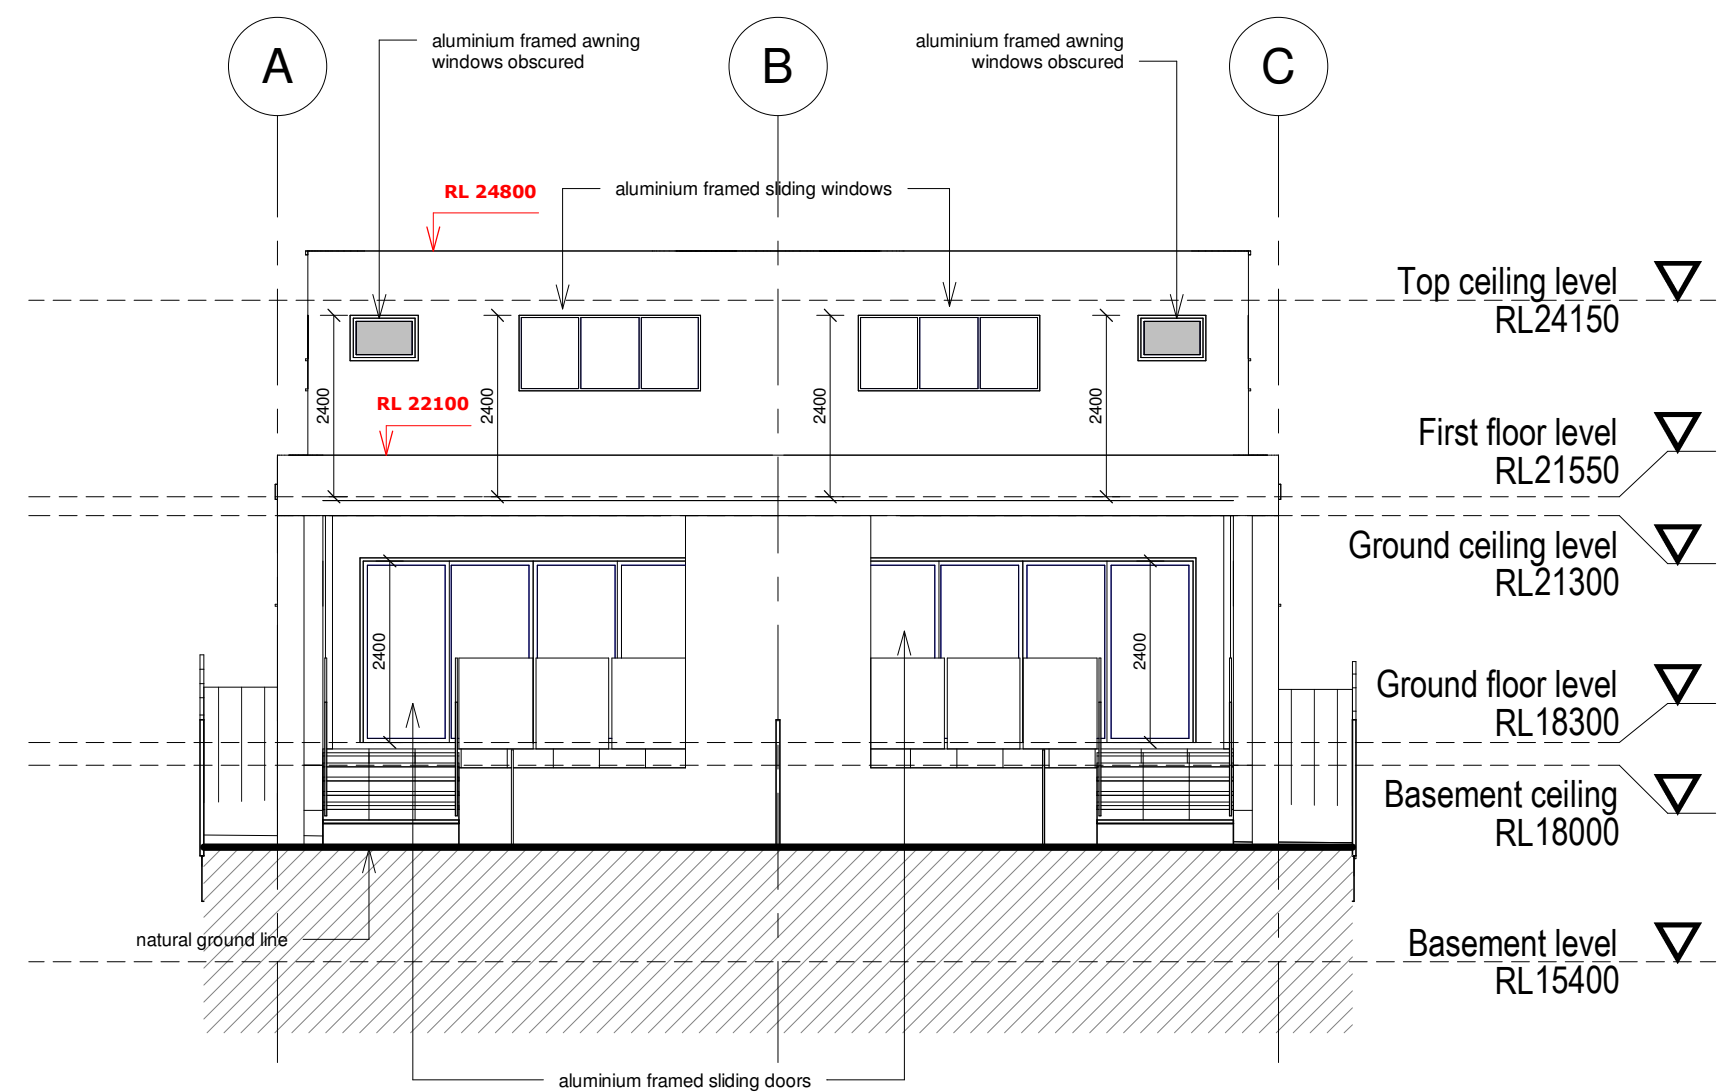

2 West elevation
1 : 100

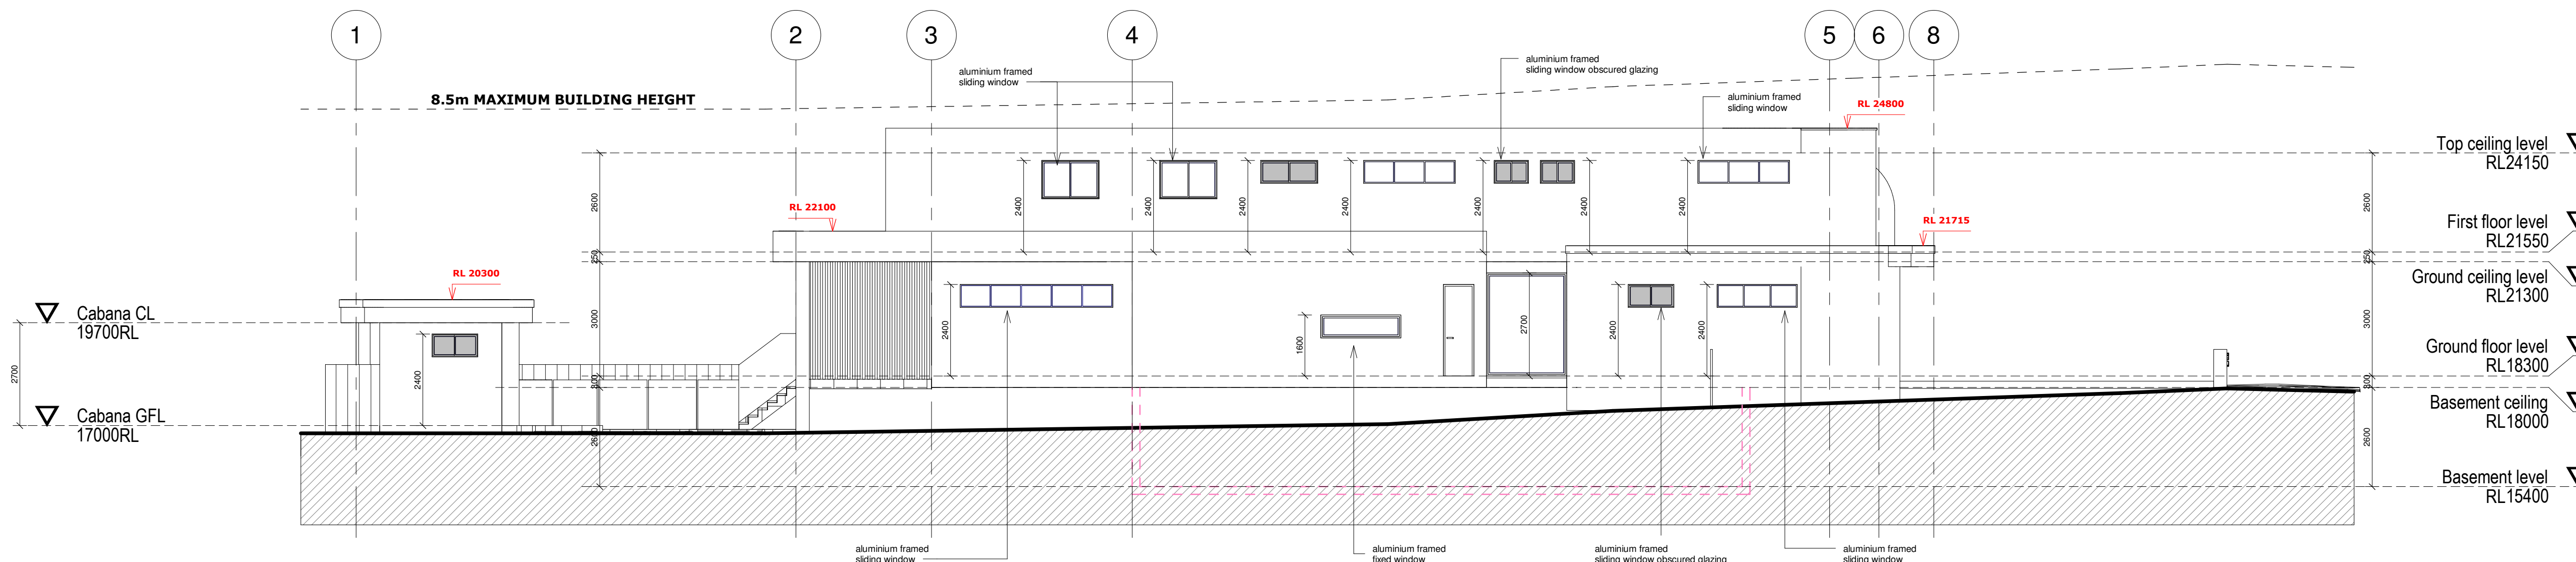

3 North elevation
1 : 100



SHOP 1, 23-27 PATON STREET,
MERRYLANDS WEST, NSW 2160
(02) 9637 1111
jack@dvyne.com.au
www.dvyne.com.au
DESIGN | CONSTRUCT | CONSULT

JOB DESCRIPTION
Proposed duplex with Basement
AT
20 Kingston Ave. Concord

DRAWING TITLE
ELEVATIONS
CLIENT DETAILS
MANORBUILD p/I


DO NOT SCALE THE DRAWINGS. READ ALL DIMENSIONS SHOWN.
ALL DIMENSIONS, NOTES ON ALL PLANS AND CONSENT
DOCUMENTS MUST BE CHECKED AND VERIFIED BY THE
CONTRACTOR PRIOR TO ANY COMMENCEMENT OF ANY
BUILDING WORKS ON SITE, TO CLARIFY ANY DISCREPANCIES
BETWEEN ALL PLAN DRAWINGS AND DOCUMENTATION RELEVANT TO THE
PROPOSAL / SITE WORKS. GROUND LEVELS MAY VARY DUE TO SITE
CONDITIONS. COPYRIGHT - THESE DRAWINGS REMAIN THE PROPERTY OF
DVYNE DESIGN. JT PTY LTD AND CAN NOT BE ALTERED OR REPRODUCED
WITHOUT WRITTEN CONSENT.

DRAWN JT
DATE DEC 2025
CHECKED JACK
SCALE 1:100
JOB NUMBER 25251-00
NUMBER IN SET A05
ISSUE A


ISSUE
A
B

AMENDMENT
CONCEPT PLAN
CDC SUBMISSION


BY JT
JH
DATE NOV 2025
DEC 2025

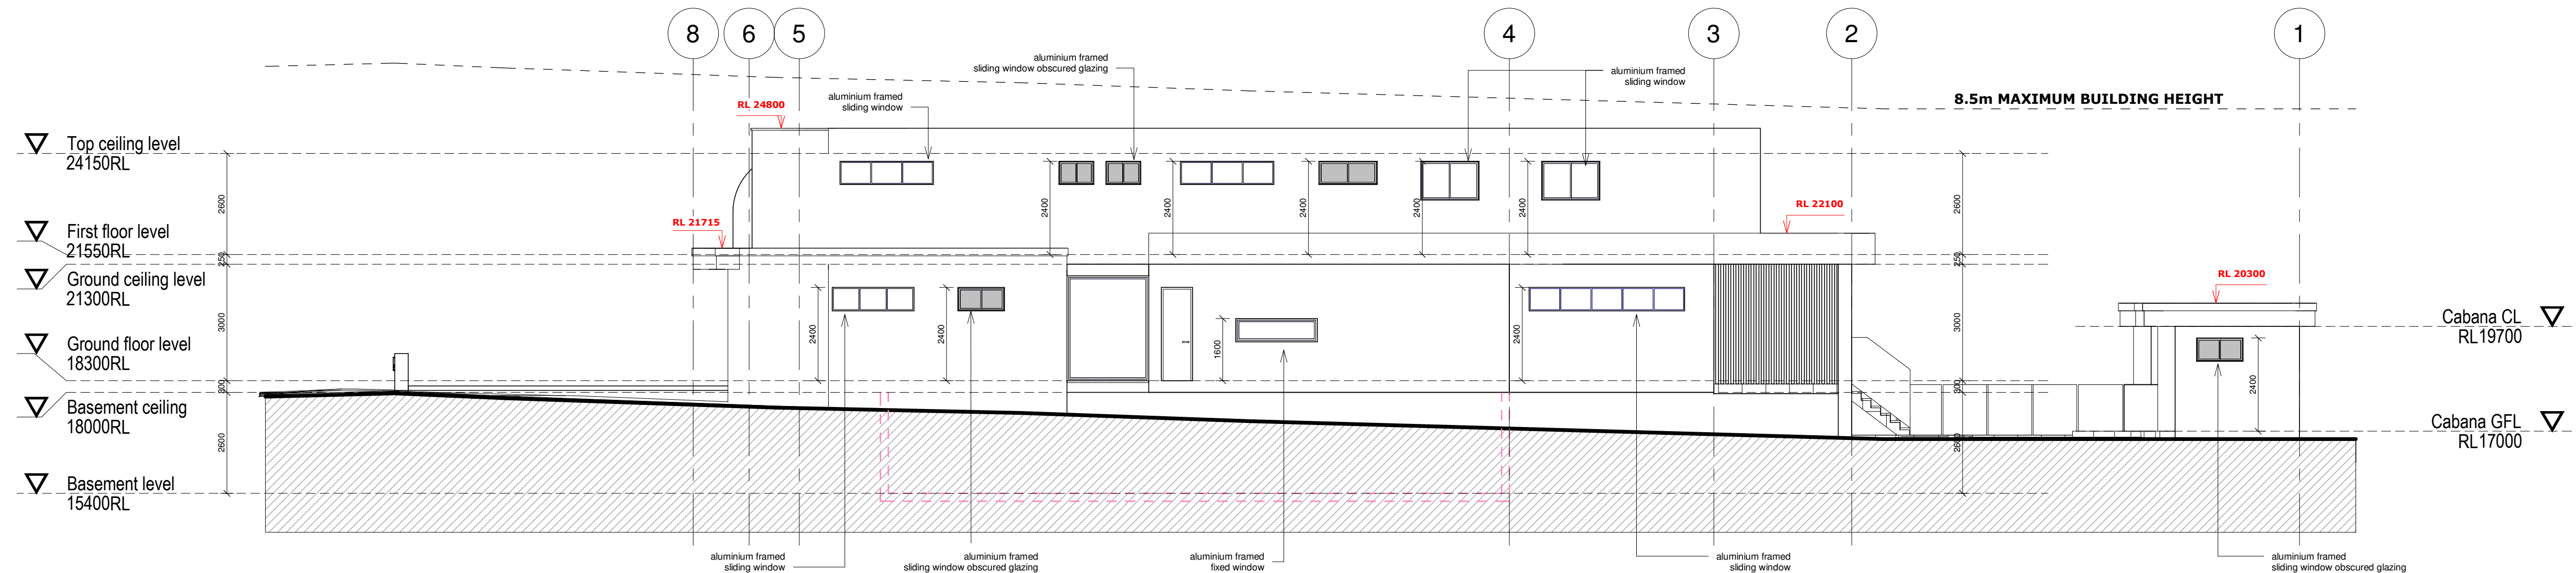


1 South elevation
1:100

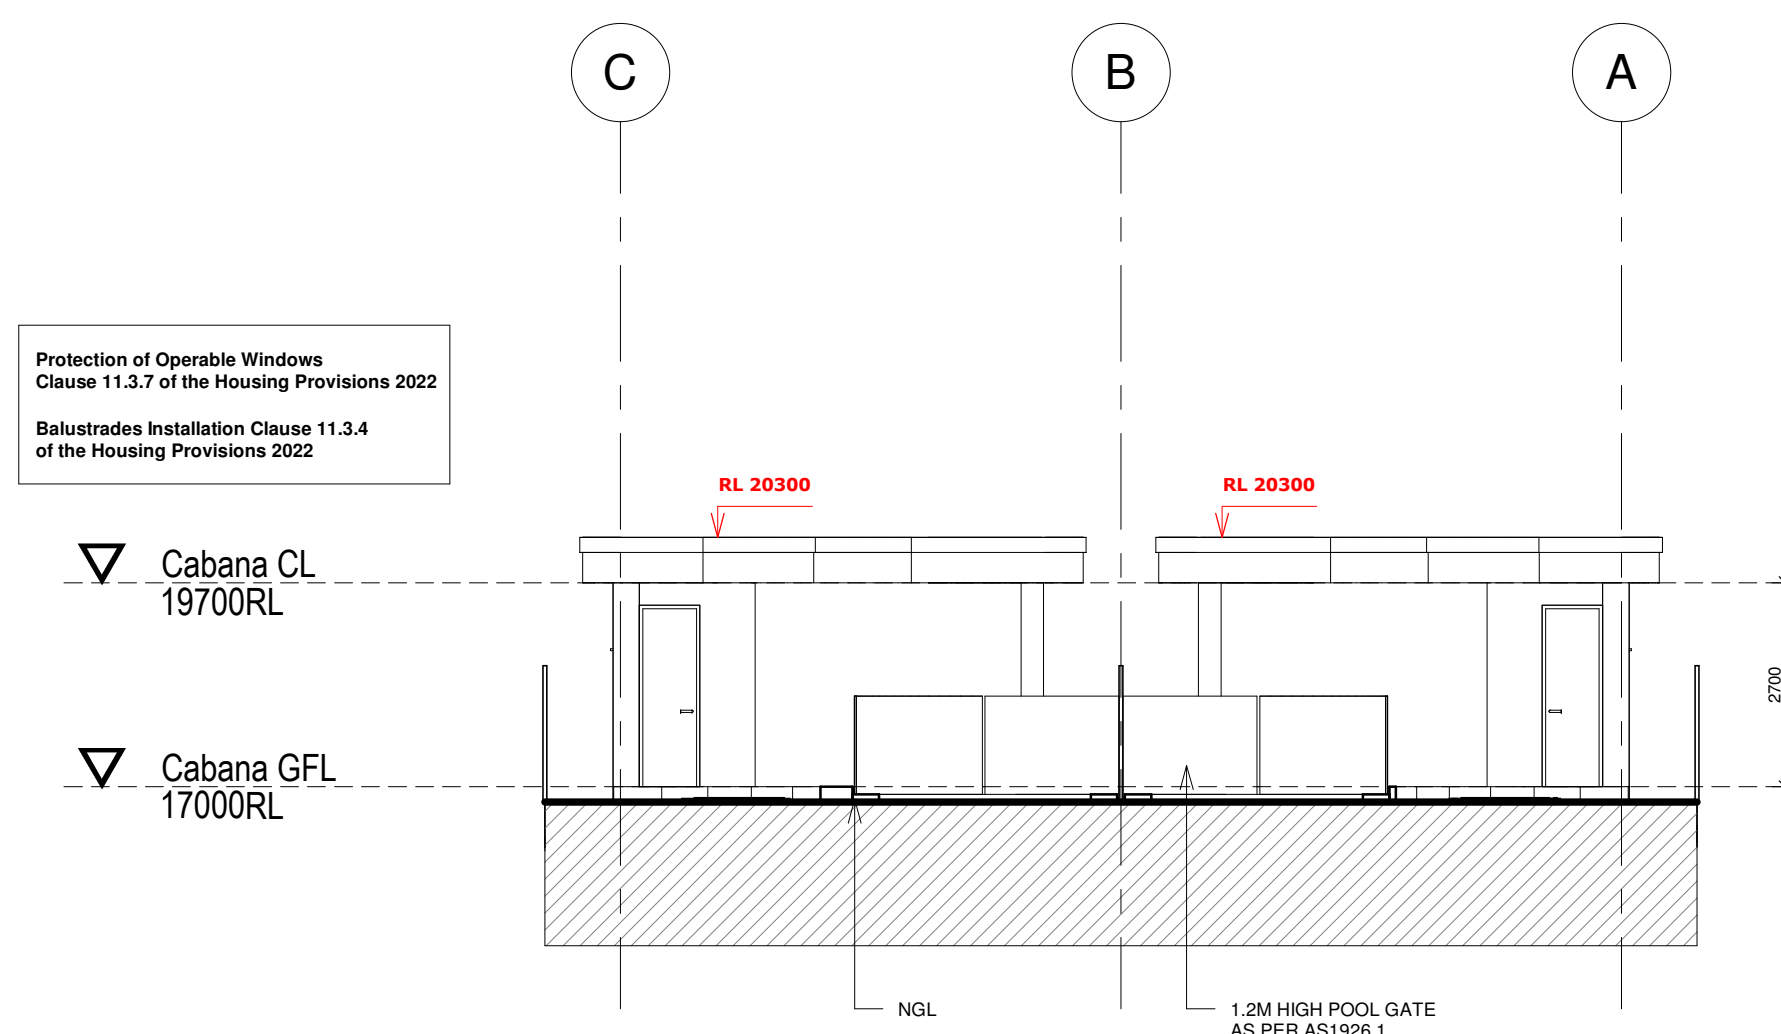

3 East Elevation 1
1:100

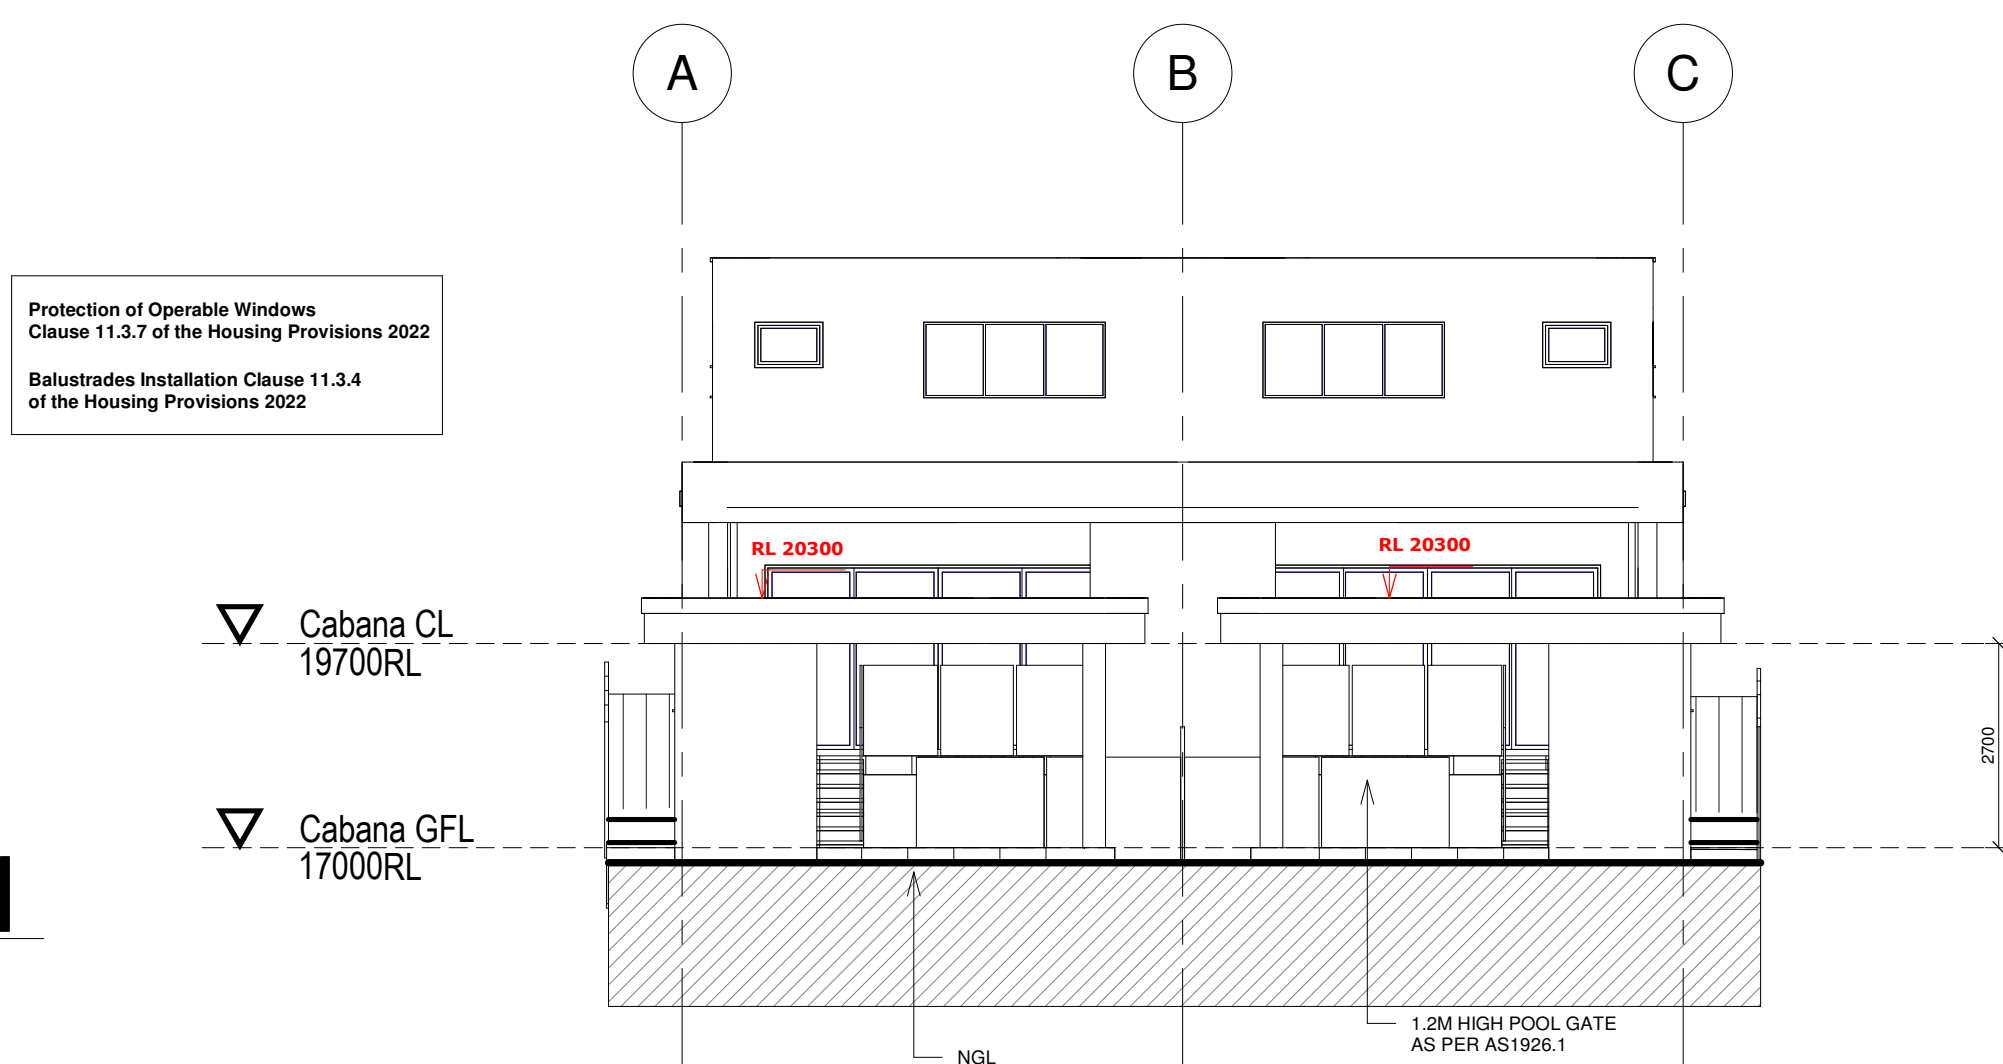

4 West Elevation 1
1:100

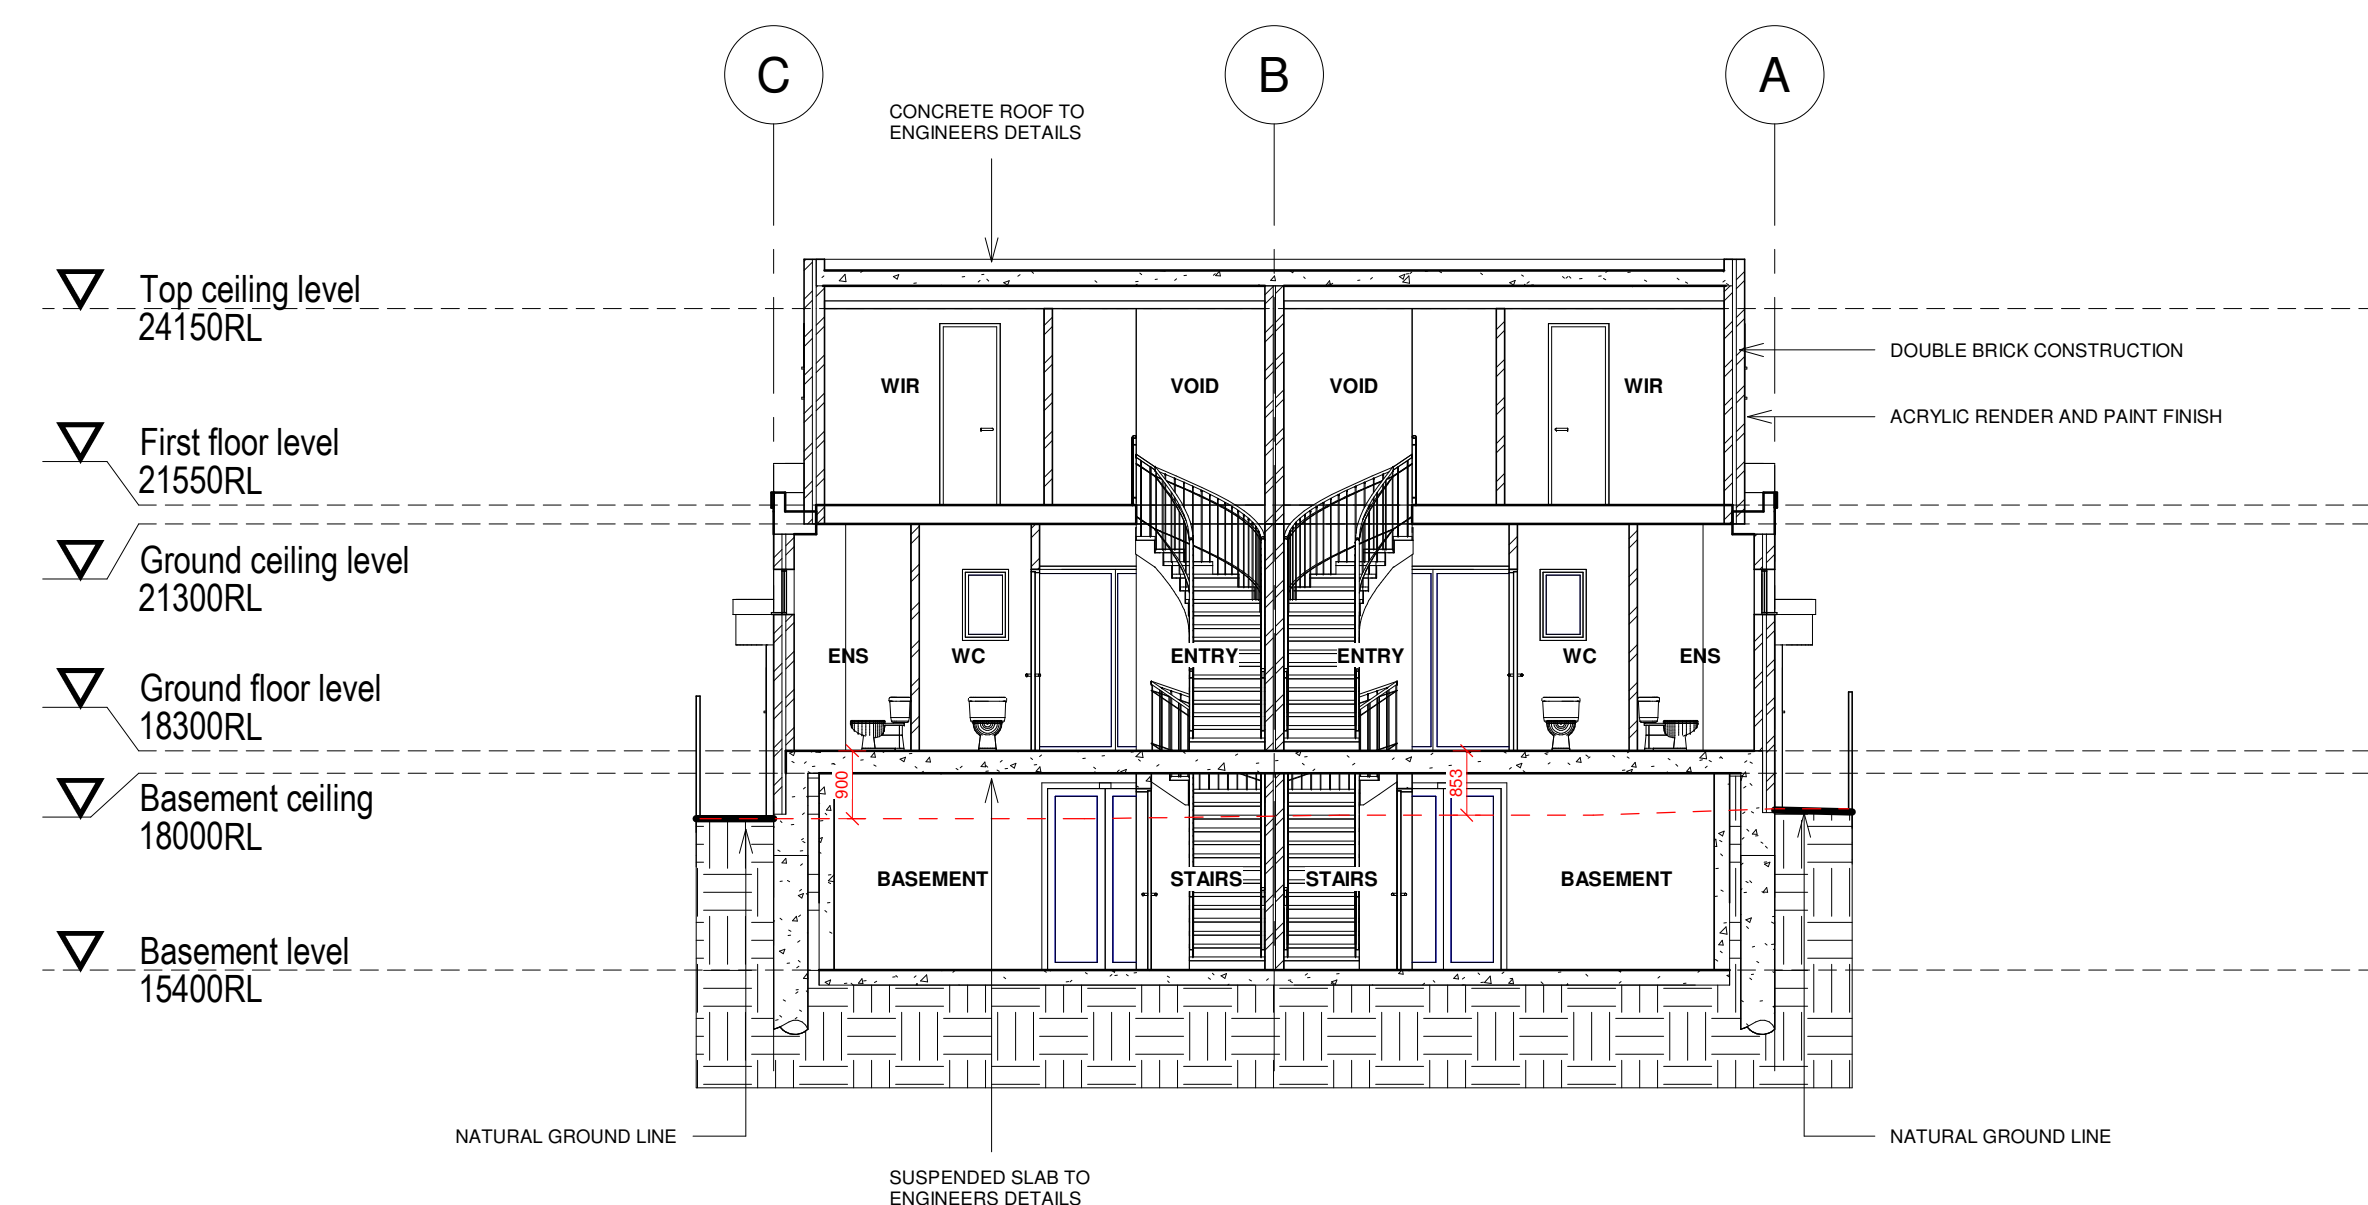

2 Section A-A
1:100



SHOP 1, 23-27 PATON STREET,
MERRYLANDS WEST, NSW 2160
(02) 9637 1111
jack@dvyne.com.au
www.dvyne.com.au
DESIGN | CONSTRUCT | CONSULT

JOB DESCRIPTION
Proposed duplex with Basement
AT
20 Kingston Ave. Concord

DRAWING TITLE
ELEVATIONS / SECTIONS
CLIENT DETAILS
MANORBUILD p/l

DO NOT SCALE THE DRAWINGS. READ ALL DIMENSIONS SHOWN.
ALL DIMENSIONS, NOTES ON ALL PLANS AND CONSENT
DOCUMENTS MUST BE CHECKED AND VERIFIED BY THE
CONTRACTOR PRIOR TO ANY COMMENCEMENT OF ANY
BUILDING WORKS ON SITE, TO CLARIFY ANY DISCREPANCIES
BETWEEN ALL PLAN DRAWINGS AND DOCUMENTATION RELEVANT TO THE
PROPOSAL / SITE WORKS. GROUND LEVELS MAY VARY DUE TO SITE
CONDITIONS. COPYRIGHT - THESE DRAWINGS REMAIN THE PROPERTY OF
Dvyne Design JT PTY LTD AND CAN NOT BE ALTERED OR REPRODUCED
WITHOUT WRITTEN CONSENT.

DRAWN JT
DATE DEC 2025
CHECKED JACK
SCALE 1:100
JOB NUMBER 25251-00
NUMBER IN SET A06
ISSUE A

ISSUE
A
B

AMENDMENT
CONCEPT PLAN
CDC SUBMISSION

BY JT
DATE NOV 2025
JH DEC 2025

BASIX COMMITMENTS - UNIT 1

Water Commitments	Show on DA plans	Show on CC/CDC plans & specs	Certifier check
Fixtures			
The applicant must install showerheads with a minimum rating of 4 star (> 4.5 but <= 6 L/min plus spray force and/or coverage tests) in all showers in the development.		✓	✓
The applicant must install a toilet flushing system with a minimum rating of 6 star in each toilet in the development.		✓	✓
The applicant must install taps with a minimum rating of 6 star in the kitchen in the development.		✓	
The applicant must install basin taps with a minimum rating of 6 star in each bathroom in the development.		✓	
Swimming Pool			
The swimming pool must not have a volume greater than 25 kilolitres.	✓	✓	
The swimming pool must be outdoors.	✓	✓	

Thermal Performance and Materials commitments	Show on DA plans	Show on CC/CDC plans & specs	Certifier check
Do-it-yourself Method			
General features			
The dwelling must be a Class 1 dwelling according to the National Construction Code, and must not have more than 2 storeys.	✓	✓	✓
The conditioned floor area of the dwelling must not exceed 300 square metres.	✓	✓	✓
The dwelling must not contain open mezzanine area exceeding 25 square metres.	✓	✓	✓
The dwelling must not contain third level habitable attic room.	✓	✓	✓
Floor, walls and ceiling/roof			
The applicant must construct the floor(s), walls, and ceiling/roof of the dwelling in accordance with the specifications listed in the table below.	✓	✓	✓
The applicant must adopt one of the options listed in the tables below to address thermal bridging in metal framed floor(s), walls and ceiling/roof of the dwelling.	✓	✓	✓
The applicant must show through receipts that the materials purchased for construction are consistent with the specifications listed in the tables below.			✓

Construction	Area - m²	Additional insulation required	Options to address thermal bridging	Other specifications
floor - concrete slab on ground, conventional slab.	129.12	nil/not specified	nil	
garage floor - concrete slab on ground.	18	none	nil	
external wall: cavity brick; frame: timber - H2 treated softwood.	all external walls	0.50 (or 1.20 including construction)fibreglass batts or roll	nil	wall colour: Medium (solar absorptance 0.48-0.7)

Construction	Area - m²	Additional insulation required	Options to address thermal bridging	Other specifications
internal wall shared with garage: 200 mm AAC block; frame: timber - H2 treated softwood.	5	nil/fibreglass batts or roll	nil	
internal wall: single skin masonry; frame: timber - H2 treated softwood.	20	fibreglass batts or roll	nil	
ceiling and roof - flat ceiling / flat roof, concrete - bare internal; timber - H2 treated softwood.	183.43	insulation over concrete ceiling: fibreglass batts or roll; roof: not specified.	nil	roof colour: medium (solar absorptance 0.48-0.58); ceiling area fully insulated

Note	• Insulation specified in this Certificate must be installed in accordance with the ABCB Housing Provisions (Part 13.2.2) of the National Construction Code.
Note	• If the additional ceiling insulation listed in the table above is greater than R3.0, refer to the ABCB Housing Provisions (Part 13.2.3 (6)) of the National Construction Code.
Note	• In some climate zones, insulation should be installed with due consideration of condensation and associated interaction with adjoining building materials.
Note	• Thermal breaks must be installed in metal framed walls and applicable roofs in accordance with the ABCB Housing Provisions of the National Construction Code.

Thermal Performance and Materials commitments	Show on DA plans	Show on CC/CDC plans & specs	Certifier check
Ceiling fans			
The applicant must install at least one ceiling fan in at least one daytime habitable space, such as living room.	✓	✓	✓
• The minimum number and diameter of ceiling fans in a daytime habitable space must be installed in accordance with the ABCB Housing Provisions (Part 13.5.2) of the National Construction Code.	✓	✓	✓

Thermal Performance and Materials commitments	Show on DA plans	Show on CC/CDC plans & specs	Certifier check
Glazed windows, doors and skylights			
The applicant must install the windows, glazed doors and shading devices described in the table below, in accordance with the specifications listed in the table. Relevant overshadowing specifications must be satisfied for each glazed window and door.	✓	✓	✓
The dwelling may have 1 skylight (<0.7 square metres) which is not listed in the table.	✓	✓	✓
The following requirements must also be satisfied in relation to each window and glazed door:	✓	✓	✓
• The applicant must install windows and glazed doors in accordance with the height and width, frame and glazing types listed in the table.	✓	✓	✓
• Each window and glazed door must have a U-value no greater than that listed and a Solar Heat Gain Coefficient (SHGC) within the range listed. Total system U values and SHGC must be calculated in accordance with National Fenestration Rating Council (NFRC) conditions.		✓	✓
The applicant must install the skylights described in the table below, in accordance with the specifications listed in the table. Total skylight area must not exceed 3 square metres (the 3 square metre limit does not include the optional additional skylight of less than 0.7 square metres that does not have to be listed in the table).	✓	✓	✓

Energy Commitments	Show on DA plans	Show on CC/CDC plans & specs	Certifier check
Hot water			
The applicant must install the following hot water system in the development, or a system with a higher energy rating: gas boosted solar with a performance of more than 45 STCs.	✓	✓	✓
Cooling system			
The applicant must install the following cooling system, or a system with a higher energy rating, in at least 1 living area: 1-phase airconditioning - ducted; Energy rating: 7 star (average zone)		✓	✓
The applicant must install the following cooling system, or a system with a higher energy rating, in at least 1 bedroom: 1-phase airconditioning - ducted; Energy rating: 7 star (average zone)		✓	✓
Heating system			
The applicant must install the following heating system, or a system with a higher energy rating, in at least 1 living area: 1-phase airconditioning - ducted; Energy rating: 7 star (average zone)		✓	✓
The applicant must install the following heating system, or a system with a higher energy rating, in at least 1 bedroom: 1-phase airconditioning - ducted; Energy rating: 7 star (average zone)		✓	✓
Ventilation			
The applicant must install the following exhaust systems in the development: At least 1 Bathroom: individual fan, open to façade; Operation control: manual switch on/off		✓	✓
Kitchen: individual fan, open to façade; Operation control: manual switch on/off		✓	✓
Laundry: individual fan, open to façade; Operation control: manual switch on/off		✓	✓
Artificial lighting			
The applicant must ensure that a minimum of 80% of light fixtures are fitted with fluorescent, compact fluorescent, or light-emitting-diode (LED) lamps.		✓	✓
Natural lighting			
The applicant must install a window and/or skylight in 6 bathroom(s)/toilet(s) in the development for natural lighting.	✓	✓	✓

Energy Commitments	Show on DA plans	Show on CC/CDC plans & specs	Certifier check
Swimming pool			
The applicant must install the following heating system for the swimming pool in the development (or alternatively must not install any heating system for the swimming pool): solar only		✓	
The applicant must install the following pump for the swimming pool in the development, or a pump with a higher energy rating: multi-speed with a performance of 8 stars or higher.		✓	
The applicant must install a timer for the swimming pool pump in the development.		✓	
Other			
The applicant must install a gas cooktop & electric oven in the kitchen of the dwelling.		✓	
The applicant must install a fixed outdoor clothes drying line as part of the development.		✓	

Legend
In these commitments, "applicant" means the person carrying out the development.
Commitments identified with a ✓ in the "Show on DA plans" column must be shown on the plans accompanying the development application for the proposed development (if a development application is to be lodged for the proposed development).
Commitments identified with a ✓ in the "Show on CC/CDC plans and specs" column must be shown in the plans and specifications accompanying the application for a construction certificate / complying development certificate for the proposed development.
Commitments identified with a ✓ in the "Certifier check" column must be certified by a certifying authority as having been fulfilled, before a final occupation certificate (either interim or final) for the development may be issued.

BASIX COMMITMENTS - UNIT 2

Water Commitments	Show on DA plans	Show on CC/CDC plans & specs	Certifier check
Fixtures			
The applicant must install showerheads with a minimum rating of 4 star (> 4.5 but <= 6 L/min plus spray force and/or coverage tests) in all showers in the development.		✓	✓
The applicant must install a toilet flushing system with a minimum rating of 6 star in each toilet in the development.		✓	✓
The applicant must install taps with a minimum rating of 6 star in the kitchen in the development.		✓	
The applicant must install basin taps with a minimum rating of 6 star in each bathroom in the development.		✓	
Swimming Pool			
The swimming pool must not have a volume greater than 25 kilolitres.	✓	✓	
The swimming pool must be outdoors.	✓	✓	

Thermal Performance and Materials commitments	Show on DA plans	Show on CC/CDC plans & specs	Certifier check
Do-it-yourself Method			
General features			
The dwelling must be a Class 1 dwelling according to the National Construction Code, and must not have more than 2 storeys.	✓	✓	✓
The conditioned floor area of the dwelling must not exceed 300 square metres.	✓	✓	✓
The dwelling must not contain open mezzanine area exceeding 25 square metres.	✓	✓	✓
The dwelling must not contain third level habitable attic room.	✓	✓	✓
Floor, walls and ceiling/roof			
The applicant must construct the floor(s), walls, and ceiling/roof of the dwelling in accordance with the specifications listed in the table below.	✓	✓	✓
The applicant must adopt one of the options listed in the tables below to address thermal bridging in metal framed floor(s), walls and ceiling/roof of the dwelling.	✓	✓	✓
The applicant must show through receipts that the materials purchased for construction are consistent with the specifications listed in the tables below.			✓

Construction	Area - m²	Additional insulation required	Options to address thermal bridging	Other specifications
floor - concrete slab on ground, conventional slab.	129.12	nil/not specified	nil	
garage floor - concrete slab on ground.	18	none	nil	
external wall: cavity brick; frame: timber - H2 treated softwood.	all external walls	0.50 (or 1.20 including construction)fibreglass batts or roll	nil	wall colour: Medium (solar absorptance 0.48-0.7)

Construction	Area - m²	Additional insulation required	Options to address thermal bridging	Other specifications
internal wall shared with garage: 200 mm AAC block; frame: timber - H2 treated softwood.	5	nil/fibreglass batts or roll	nil	
internal wall: single skin masonry; frame: timber - H2 treated softwood.	20	fibreglass batts or roll	nil	
ceiling and roof - flat ceiling / flat roof, concrete - bare internal; timber - H2 treated softwood.	183.43	insulation over concrete ceiling: fibreglass batts or roll; roof: not specified.	nil	roof colour: medium (solar absorptance 0.48-0.58); ceiling area fully insulated

Note	• Insulation specified in this Certificate must be installed in accordance with the ABCB Housing Provisions (Part 13.2.2) of the National Construction Code.
Note	• If the additional ceiling insulation listed in the table above is greater than R3.0, refer to the ABCB Housing Provisions (Part 13.2.3 (6)) of the National Construction Code.
Note	• In some climate zones, insulation should be installed with due consideration of condensation and associated interaction with adjoining building materials.
Note	• Thermal breaks must be installed in metal framed walls and applicable roofs in accordance with the ABCB Housing Provisions of the National Construction Code.

Thermal Performance and Materials commitments	Show on DA plans	Show on CC/CDC plans & specs	Certifier check
Ceiling fans			
The applicant must install at least one ceiling fan in at least one daytime habitable space, such as living room.	✓	✓	✓
• The minimum number and diameter of ceiling fans in a daytime habitable space must be installed in accordance with the ABCB Housing Provisions (Part 13.5.2) of the National Construction Code.	✓	✓	✓

Thermal Performance and Materials commitments	Show on DA plans	Show on CC/CDC plans & specs	Certifier check
Glazed windows, doors and skylights			
The applicant must install the windows, glazed doors and shading devices described in the table below, in accordance with the specifications listed in the table. Relevant overshadowing specifications must be satisfied for each glazed window and door.	✓	✓	✓
The dwelling may have 1 skylight (<0.7 square metres) which is not listed in the table.	✓	✓	✓
The following requirements must also be satisfied in relation to each window and glazed door:	✓	✓	✓
• The applicant must install windows and glazed doors in accordance with the height and width, frame and glazing types listed in the table.	✓	✓	✓
• Each window and glazed door must have a U-value no greater than that listed and a Solar Heat Gain Coefficient (SHGC) within the range listed. Total system U values and SHGC must be calculated in accordance with National Fenestration Rating Council (NFRC) conditions.		✓	✓
The applicant must install the skylights described in the table below, in accordance with the specifications listed in the table. Total skylight area must not exceed 3 square metres (the 3 square metre limit does not include the optional additional skylight of less than 0.7 square metres that does not have to be listed in the table).	✓	✓	✓

Energy Commitments	Show on DA plans	Show on CC/CDC plans & specs	Certifier check
Hot water			
The applicant must install the following hot water system in the development, or a system with a higher energy rating: gas boosted solar with a performance of more than 45 STCs.	✓	✓	✓
Cooling system			
The applicant must install the following cooling system, or a system with a higher energy rating, in at least 1 living area: 1-phase airconditioning - ducted; Energy rating: 7 star (average zone)		✓	✓
The applicant must install the following cooling system, or a system with a higher energy rating, in at least 1 bedroom: 1-phase airconditioning - ducted; Energy rating: 7 star (average zone)		✓	✓
Heating system			
The applicant must install the following heating system, or a system with a higher energy rating, in at least 1 living area: 1-phase airconditioning - ducted; Energy rating: 7 star (average zone)		✓	✓
The applicant must install the following heating system, or a system with a higher energy rating, in at least 1 bedroom: 1-phase airconditioning - ducted; Energy rating: 7 star (average zone)		✓	✓
Ventilation			
The applicant must install the following exhaust systems in the development: At least 1 Bathroom: individual fan, open to façade; Operation control: manual switch on/off		✓	✓
Kitchen: individual fan, open to façade; Operation control: manual switch on/off		✓	✓
Laundry: individual fan, open to façade; Operation control: manual switch on/off		✓	✓
Artificial lighting			
The applicant must ensure that a minimum of 80% of light fixtures are fitted with fluorescent, compact fluorescent, or light-emitting-diode (LED) lamps.		✓	✓
Natural lighting			
The applicant must install a window and/or skylight in 6 bathroom(s)/toilet(s) in the development for natural lighting.	✓	✓	✓

Energy Commitments	Show on DA plans	Show on CC/CDC plans & specs	Certifier check
Swimming pool			
The applicant must install the following heating system for the swimming pool in the development (or alternatively must not install any heating system for the swimming pool): solar only		✓	
The applicant must install the following pump for the swimming pool in the development, or a pump with a higher energy rating: multi-speed with a performance of 8 stars or higher.		✓	
The applicant must install a timer for the swimming pool pump in the development.		✓	
Other			
The applicant must install a gas cooktop & electric oven in the kitchen of the dwelling.		✓	
The applicant must install a fixed outdoor clothes drying line as part of the development.		✓	

Legend
In these commitments, "applicant" means the person carrying out the development.
Commitments identified with a ✓ in the "Show on DA plans" column must be shown on the plans accompanying the development application for the proposed development (if a development application is to be lodged for the proposed development).
Commitments identified with a ✓ in the "Show on CC/CDC plans and specs" column must be shown in the plans and specifications accompanying the application for a construction certificate / complying development certificate for the proposed development.
Commitments identified with a ✓ in the "Certifier check" column must be certified by a certifying authority as having been fulfilled, before a final occupation certificate (either interim or final) for the development may be issued.



SHOP 1, 23-27 PATON STREET,
MERRYLANDS WEST, NSW 2160
(02) 9637 1111
jack@dvyne.com.au
www.dvyne.com.au
DESIGN | CONSTRUCT | CONSULT

JOB DESCRIPTION
Proposed duplex with Basement
AT
20 Kingston Ave. Concord

DRAWING TITLE
SURFACE TREATMENT / BASIX
CLIENT DETAILS
MANORBUILD p/I

DO NOT SCALE THE DRAWINGS. READ ALL DIMENSIONS SHOWN.
ALL DIMENSIONS, NOTES ON ALL PLANS AND CONSENT DOCUMENTS MUST BE CHECKED AND VERIFIED BY THE CONTRACTOR PRIOR TO ANY COMMENCEMENT OF ANY BUILDING WORKS ON SITE, TO CLARIFY ANY DISCREPANCIES BETWEEN ALL PLAN DRAWINGS AND DOCUMENTATION RELEVANT TO THE PROPOSAL / SITE WORKS. GROUND LEVELS MAY VARY DUE TO SITE CONDITIONS. COPYRIGHT - THESE DRAWINGS REMAIN THE PROPERTY OF DVYNE DESIGN JT PTY LTD AND CAN NOT BE ALTERED OR REPRODUCED WITHOUT WRITTEN CONSENT.

DRAWN	JT
DATE	DEC 2025
CHECKED	JACK
SCALE	1:100
JOB NUMBER	25251-00
NUMBER IN SET	A07
ISSUE	A

ISSUE
A
B

AMENDMENT
CONCEPT PLAN
CDC SUBMISSION

BY	DATE
JT	NOV 2025
JH	DEC 2025

