

PROPOSED NEW SINGLE STOREY DWELLING


Lot: 4420, No.11 Walla Walla Way, Menangle Park. NSW 2563



FIGURED DIMENSIONS TO BE USED IN
PREFERENCE TO SCALING THIS DRAWING
DO NOT ASSUME - IF IN DOUBT ASK.



BUSHFIRE BAL-12.5
(In Compliance with AS3959-2018)

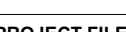 TAYLORED DESIGNS & DRAFTING Phone: 0401 482 401 Email: info@taylorreddesigns.com.au Copyright. © This plan is the property of Taylorred Designs & Drafting and may not be used in whole or part		GENERAL NOTES 1. LEVELS SHOWN ARE APPROXIMATE AND TO BE CONFIRMED ON SITE BY SURVEYOR. 2. ENGINEERS DRAWINGS ARE REQUIRED AND THOSE DRAWINGS MUST TAKE PREFERENCE TO THESE DRAWINGS 3. ALL BOUNDARY CLEARANCES MUST BE VERIFIED BEFORE COMMENCEMENT OF BUILDING WORKS BY REGISTERED SURVEYOR. 4. BUILDER IS TO STRICTLY COMPLY WITH ALL RELEVANT BUILDING CODE OF AUSTRALIA CONSTRUCTION REQUIREMENTS AND AUSTRALIAN STANDARDS. 5. IN CASE OF ALTERATIONS OR DISCREPANCIES NOTIFY TAYLORED DESIGNS & DRAFTING IMMEDIATELY.		REF: A 08.07.26 PRELIMINARY PLANS B 23.07.26 DRP AMENDMENTS C 21.08.26 CDC PLANS		AMENDMENT:		PROPOSED: SINGLE STOREY DWELLING		CLIENT:	
								ELA Projects Pty Ltd			
						AT: Lot: 4420, DP: 1313734 No.11 Walla Walla Way, Menangle Park. NSW 2563		PROJECT FILES 		JOB NO: 260120 DATE: 08.07.26 DRAWN: MT	
								Sheet Size: A2 LGA: Campbelltown City Sheet: COVER SHEET			

Existing Site Plan
1:200

Proposed Site Plan
1:200

LOT 4420
DP: 1313734
425.30m²

LOT 4420
DP: 1313734
425.30m²



LEGEND:

AHD	AUSTRALIAN HEIGHT DATUM
AWN	AWNING
BM	BENCH MARK
CL	CENTRE LINE
CONC	CONCRETE
CS	CONCRETE SURFACE
D/H/S	DIAMETER/HEIGHT/SPREAD
D	DOOR
EC	EDGE OF CONCRETE
EG	EAVE & GUTTER
EP	ELECTRICAL BOX
FL	FLOOR LEVEL
GDN	GARDEN
HYD	HYDRANT
IC	INSPECTION COVER
INV	INVERT LEVEL
KO	KERB OUTLET
LH	LAMP HOLE
LIP	LIP OF KERB
NS	NATURAL SURFACE
PAV	PAVERS
PP	POWER POLE
RL	REDUCED LEVEL
S	STEPS
SL	SURFACE LEVEL
SILL	WINDOW SILL
SIP	SEWER INSPECTION POINT
SMH	SEWER MAN HOLE
SV	STOP VALE
TEL	TELSTRA PIT
TK	TOP OF KERB
TOW/TW	TOP OF WALL
TRW	TOP OF RETAINING WALL
VC	VEHICLE CROSSING
WM	WATER METER
WTOP	TOP OF WINDOW

LEGEND:

AHD	AUSTRALIAN HEIGHT DATUM
AWN	AWNING
BM	BENCH MARK
CL	CENTRE LINE
CONC	CONCRETE
CS	CONCRETE SURFACE
D/H/S	DIAMETER/HEIGHT/SPREAD
D	DOOR
EC	EDGE OF CONCRETE
EG	EAVE & GUTTER
EP	ELECTRICAL BOX
FL	FLOOR LEVEL
GDN	GARDEN
HYD	HYDRANT
IC	INSPECTION COVER
INV	INVERT LEVEL
KO	KERB OUTLET
LH	LAMP HOLE
LIP	LIP OF KERB
NS	NATURAL SURFACE
PAV	PAVERS
PP	POWER POLE
RL	REDUCED LEVEL
S	STEPS
SL	SURFACE LEVEL
SILL	WINDOW SILL
SIP	SEWER INSPECTION POINT
SMH	SEWER MAN HOLE
SV	STOP VALE
TEL	TELSTRA PIT
TK	TOP OF KERB
TOW/TW	TOP OF WALL
TRW	TOP OF RETAINING WALL
VC	VEHICLE CROSSING
WM	WATER METER
WTOP	TOP OF WINDOW

NOTES:

- A) THIS SURVEY IS SPECIFICALLY FOR CONTOUR PURPOSES ONLY. THE BOUNDARIES OF THE SUBJECT PROPERTY HAVE NOT BEEN INVESTIGATED BY US AND THE POSITION SHOWN IS APPROXIMATE ONLY.
- B) IF THE DIMENSIONS OR DESCRIPTION OF THE TITLE ARE CRITICAL FOR DESIGN AND/OR CONSTRUCTION OF NEW STRUCTURES OR FINANCIAL DECISIONS WE RECOMMEND THAT AN IDENTIFICATION SURVEY OR RE-SURVEY OF BOUNDARIES BE CARRIED OUT.
- C) SERVICES SHOWN HAVE BEEN DERIVED FROM VISUAL EVIDENCE APPARENT AT THE TIME OF SURVEY. SERVICES MAY EXIST WHICH ARE NOT SHOWN. THE RELEVANT SERVICE AUTHORITY SHOULD BE CONTACTED TO VERIFY THE EXISTENCE AND POSITION OF SERVICES PRIOR TO THE COMMENCEMENT OF ANY CONSTRUCTION OR EXCAVATION.
- D) DETAIL ON THIS PLAN HAS BEEN LOCATED FOR PLOTTING PURPOSES ONLY.
- E) DIAMETER, HEIGHT & SPREAD OF TREES ARE APPROXIMATE ONLY.
- F) LEVELS SHOWN ARE OF AUSTRALIAN HEIGHT DATUM.
- G) ORIGIN OF LEVELS: SSM 226792, RL: 88.157(AHD), CLASS LC.
- H) USE STATED DIMENSIONS. DO NOT SCALE.
- I) THESE NOTES FORM PART OF THIS PLAN AND CANNOT BE REMOVED. NO COVENANTS AND/OR RESTRICTIONS HAVE BEEN INVESTIGATED BY C & A SURVEYORS PTY LTD.

NOTES:

- A) THIS SURVEY IS SPECIFICALLY FOR CONTOUR PURPOSES ONLY. THE BOUNDARIES OF THE SUBJECT PROPERTY HAVE NOT BEEN INVESTIGATED BY US AND THE POSITION SHOWN IS APPROXIMATE ONLY.
- B) IF THE DIMENSIONS OR DESCRIPTION OF THE TITLE ARE CRITICAL FOR DESIGN AND/OR CONSTRUCTION OF NEW STRUCTURES OR FINANCIAL DECISIONS WE RECOMMEND THAT AN IDENTIFICATION SURVEY OR RE-SURVEY OF BOUNDARIES BE CARRIED OUT.
- C) SERVICES SHOWN HAVE BEEN DERIVED FROM VISUAL EVIDENCE APPARENT AT THE TIME OF SURVEY. SERVICES MAY EXIST WHICH ARE NOT SHOWN. THE RELEVANT SERVICE AUTHORITY SHOULD BE CONTACTED TO VERIFY THE EXISTENCE AND POSITION OF SERVICES PRIOR TO THE COMMENCEMENT OF ANY CONSTRUCTION OR EXCAVATION.
- D) DETAIL ON THIS PLAN HAS BEEN LOCATED FOR PLOTTING PURPOSES ONLY.
- E) DIAMETER, HEIGHT & SPREAD OF TREES ARE APPROXIMATE ONLY.
- F) LEVELS SHOWN ARE OF AUSTRALIAN HEIGHT DATUM.
- G) ORIGIN OF LEVELS: SSM 226792, RL: 88.157(AHD), CLASS LC.
- H) USE STATED DIMENSIONS. DO NOT SCALE.
- I) THESE NOTES FORM PART OF THIS PLAN AND CANNOT BE REMOVED. NO COVENANTS AND/OR RESTRICTIONS HAVE BEEN INVESTIGATED BY C & A SURVEYORS PTY LTD.

BCA (NCC) & AUSTRALIAN STANDARDS
COMPLIANCE NOTES:

EARTHWORK IS TO COMPLY WITH PART H103 OF NCC 2022 - SITE PREPARATION

TERMITE MANAGEMENT IS TO COMPLY WITH PART H103 OF NCC 2022 - SITE PREPARATION AND AS 3668.1-2014. A DURABLE NOTICE IS TO BE INSTALLED IN ACCORDANCE WITH PART H103 OF NCC 2022. WHERE A CHEMICAL TERMITE MANAGEMENT SYSTEM IS USED, THE CHEMICAL MUST BE INCLUDED ON THE APPROPRIATE AUTHORITY'S PESTICIDES REGISTER


FOOTINGS AND SLABS ARE TO COMPLY WITH AS 2870-2011.

BCA (NCC) & AUSTRALIAN STANDARDS
COMPLIANCE NOTES:

EARTHWORK IS TO COMPLY WITH PART H103 OF NCC 2022 - SITE PREPARATION

TERMITE MANAGEMENT IS TO COMPLY WITH PART H103 OF NCC 2022 - SITE PREPARATION AND AS 3668.1-2014. A DURABLE NOTICE IS TO BE INSTALLED IN ACCORDANCE WITH PART H103 OF NCC 2022. WHERE A CHEMICAL TERMITE MANAGEMENT SYSTEM IS USED, THE CHEMICAL MUST BE INCLUDED ON THE APPROPRIATE AUTHORITY'S PESTICIDES REGISTER

FOOTINGS AND SLABS ARE TO COMPLY WITH AS 2870-2011.

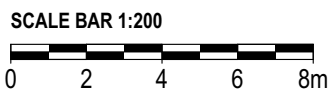

Phone: 0401 482 401 Email: info@taylorreddesigns.com.au

Copyright. © This plan is the property of Taylored Designs & Drafting and may not be used in whole or part

GENERAL NOTES

- LEVELS SHOWN ARE APPROXIMATE AND TO BE CONFIRMED ON SITE BY SURVEYOR.
- ENGINEERS DRAWINGS ARE REQUIRED AND THOSE DRAWINGS MUST TAKE PREFERENCE TO THESE DRAWINGS
- ALL BOUNDARY CLEARANCES MUST BE VERIFIED BEFORE COMMENCEMENT OF BUILDING WORKS BY REGISTERED SURVEYOR.
- BUILDER IS TO STRICTLY COMPLY WITH ALL RELEVANT BUILDING CODE OF AUSTRALIA CONSTRUCTION REQUIREMENTS AND AUSTRALIAN STANDARDS.
- IN CASE OF ALTERATIONS OR DISCREPANCIES NOTIFY TAYLORED DESIGNS & DRAFTING IMMEDIATELY.

REF:	DATE:	AMENDMENT:
A	08.07.26	PRELIMINARY PLANS
B	23.07.26	DRP AMENDMENTS
C	21.08.26	CDC PLANS

PROPOSED: SINGLE STOREY DWELLING

AT: Lot: 4420, DP: 1313734
No.11 Walla Walla Way,
Menangle Park. NSW 2563

CLIENT:
ELA Projects Pty Ltd

JOB NO: 260120 DATE: 08.07.26 DRAWN: MT

Sheet Size: A2 LGA: Campbelltown City Sheet: 1 of 9



BUSHFIRE BAL-12.5
(In Compliance with AS3959-2018)

Proposed Site Analysis Plan

1:200


LOT 4420

DP: 1313734

425.30m²

LEGEND:

AHD	AUSTRALIAN HEIGHT DATUM
AWN	AWNING
BM	BENCH MARK
CL	CENTRE LINE
CONC	CONCRETE
CS	CONCRETE SURFACE
D/H/S	DIAMETER/HEIGHT/SPREAD
D	DOOR
EC	EDGE OF CONCRETE
EG	EAVE & GUTTER
EP	ELECTRICAL BOX
FL	FLOOR LEVEL
GDN	GARDEN
HYD	HYDRANT
IC	INSPECTION COVER
INV	INVERT LEVEL
KO	KERB OUTLET
LH	LAMP HOLE
LIP	LIP OF KERB
NS	NATURAL SURFACE
PAV	PAVERS
PP	POWER POLE
RL	REDUCED LEVEL
S	STEPS
SL	SURFACE LEVEL
SILL	WINDOW SILL
SIP	SEWER INSPECTION POINT
SMH	SEWER MAN HOLE
SV	STOP VALE
TEL	TELSTRA PIT
TK	TOP OF KERB
TOW/TW	TOP OF WALL
TRW	TOP OF RETAINING WALL
VC	VEHICLE CROSSING
WM	WATER METER
WTOP	TOP OF WINDOW

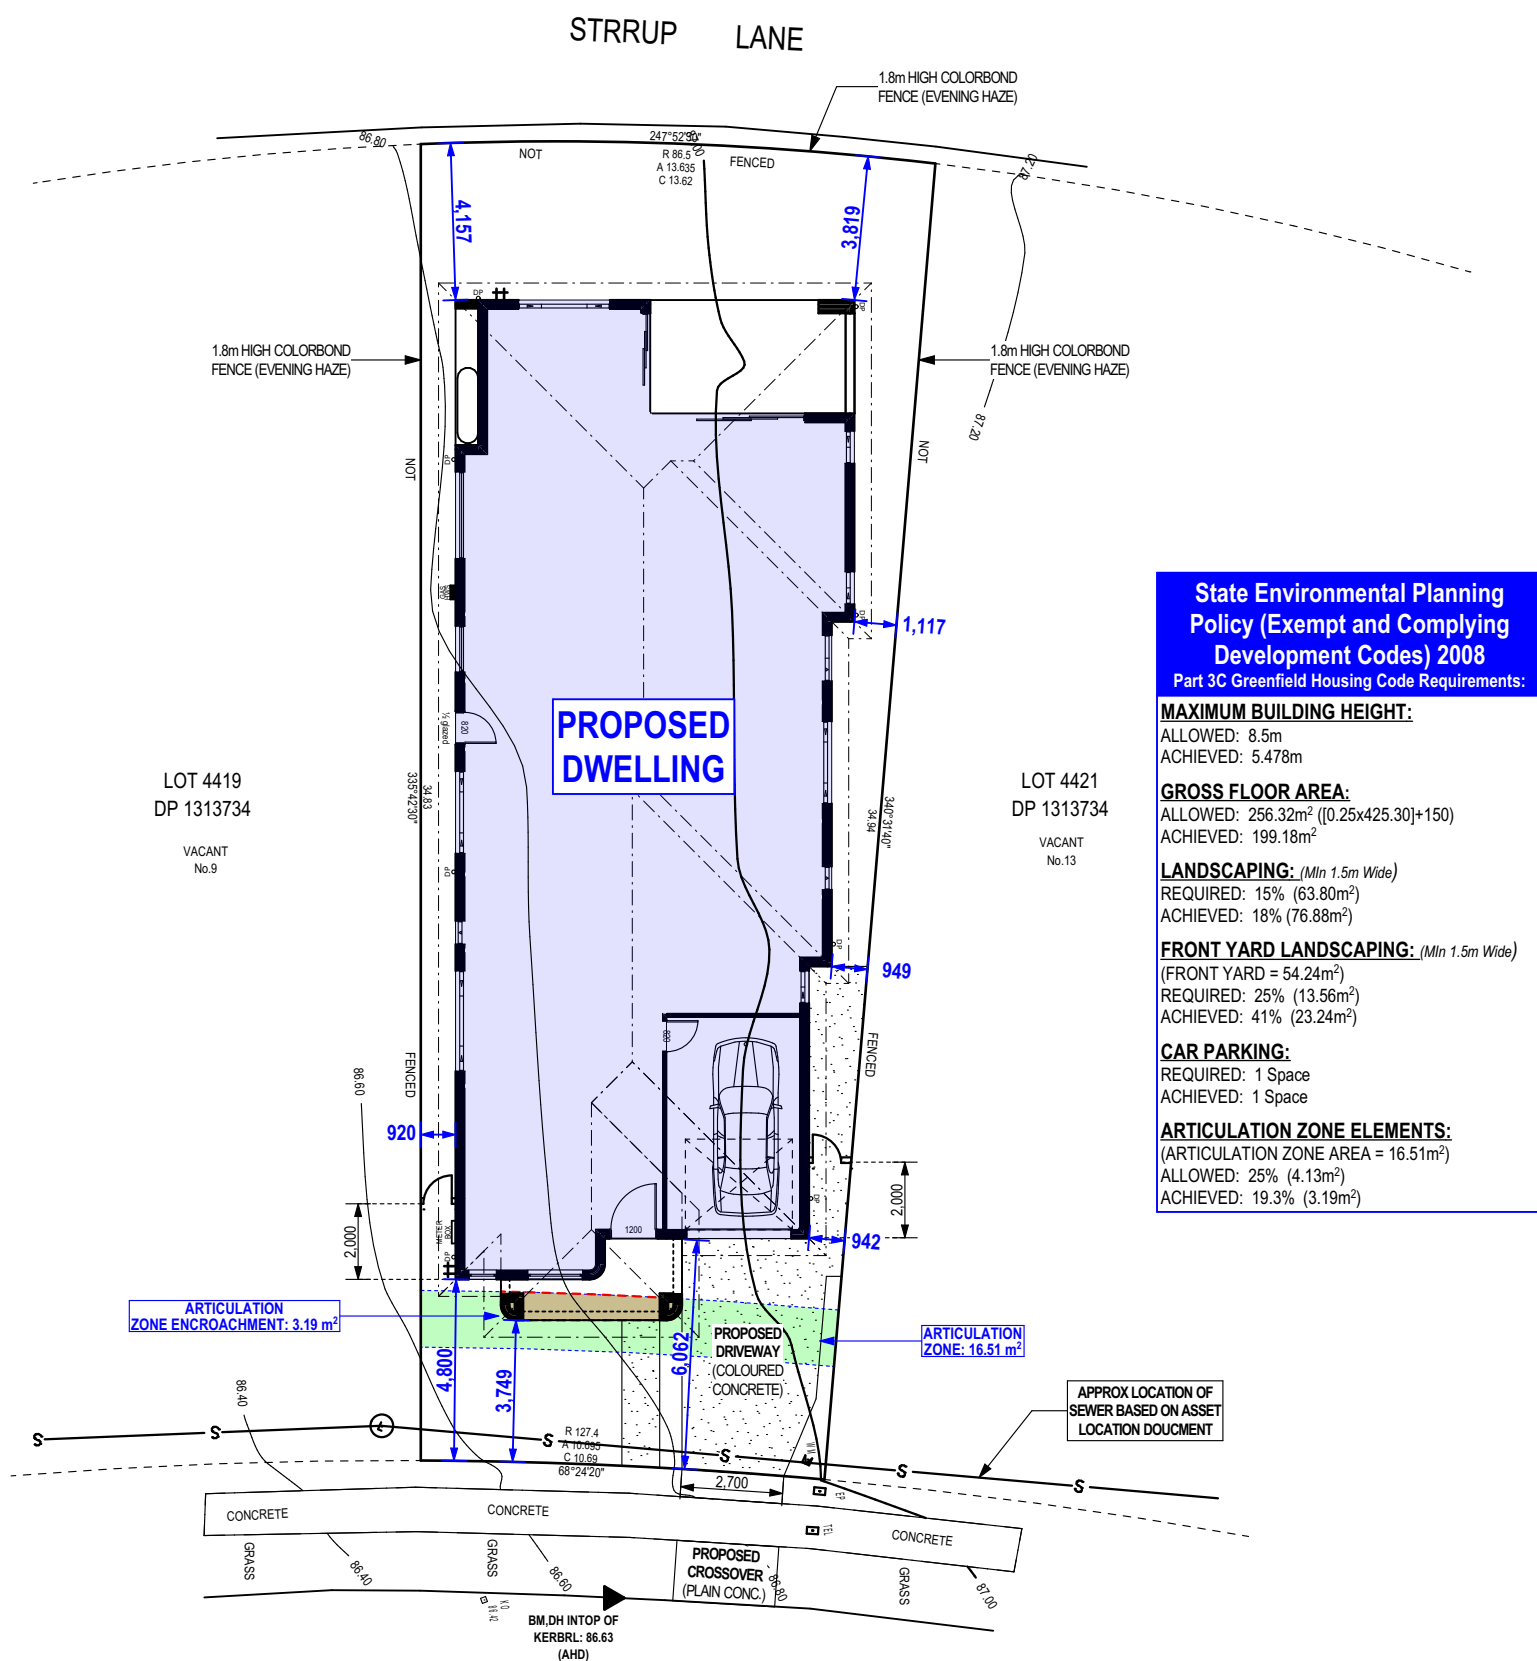State Environmental Planning Policy (Exempt and Complying Development Codes) 2008
Part 3C Greenfield Housing Code Requirements:

MAXIMUM BUILDING HEIGHT:

ALLOWED: 8.5m
ACHIEVED: 5.478m

GROSS FLOOR AREA:

ALLOWED: 256.32m² (0.25x425.30)+150
ACHIEVED: 199.18m²

LANDSCAPING: (Min 1.5m Wide)

REQUIRED: 15% (63.80m²)
ACHIEVED: 18% (76.88m²)

FRONT YARD LANDSCAPING: (Min 1.5m Wide)

(FRONT YARD = 54.24m²)
REQUIRED: 25% (13.56m²)
ACHIEVED: 41% (23.24m²)

CAR PARKING:

REQUIRED: 1 Space
ACHIEVED: 1 Space

ARTICULATION ZONE ELEMENTS:

(ARTICULATION ZONE AREA = 16.51m²)
ALLOWED: 25% (4.13m²)
ACHIEVED: 19.3% (3.19m²)


BCA (NCC) & AUSTRALIAN STANDARDS COMPLIANCE NOTES:

EARTHWORK IS TO COMPLY WITH PART H103 OF NCC 2022 - SITE PREPARATION

TERMITE MANAGEMENT IS TO COMPLY WITH PART H103 OF NCC 2022 - SITE PREPARATION AND AS 3668.1-2014. A DURABLE NOTICE IS TO BE INSTALLED IN ACCORDANCE WITH PART H103 OF NCC 2022, WHERE A CHEMICAL TERMITE MANAGEMENT SYSTEM IS USED, THE CHEMICAL MUST BE INCLUDED ON THE APPROPRIATE AUTHORITY'S PESTICIDES REGISTER

FOOTINGS AND SLABS ARE TO COMPLY WITH AS 2870-2011.

SCALE BAR 1:200

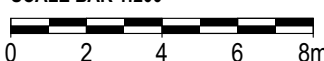

Phone: 0401 482 401

Email: info@taylorreddesigns.com.au

Copyright. ©


This plan is the property of Taylored Designs & Drafting and may not be used in whole or part

GENERAL NOTES


- LEVELS SHOWN ARE APPROXIMATE AND TO BE CONFIRMED ON SITE BY SURVEYOR.
- ENGINEERS DRAWINGS ARE REQUIRED AND THOSE DRAWINGS MUST TAKE PREFERENCE TO THESE DRAWINGS
- ALL BOUNDARY CLEARANCES MUST BE VERIFIED BEFORE COMMENCEMENT OF BUILDING WORKS BY REGISTERED SURVEYOR.
- BUILDER IS TO STRICTLY COMPLY WITH ALL RELEVANT BUILDING CODE OF AUSTRALIA CONSTRUCTION REQUIREMENTS AND AUSTRALIAN STANDARDS.
- IN CASE OF ALTERATIONS OR DISCREPANCIES NOTIFY TAYLORED DESIGNS & DRAFTING IMMEDIATELY.

Proposed Site-Works Plan

1:200

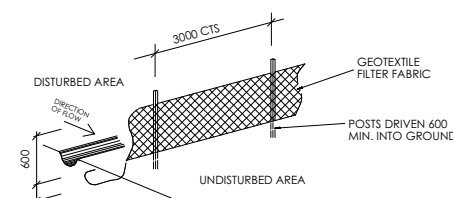

SEDIMENT CONTROL FENCE

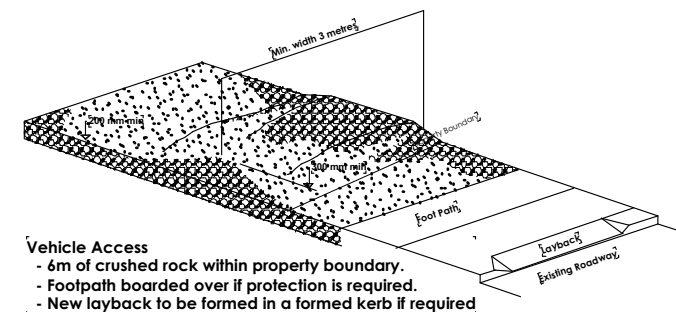

Vehicle Access
- 6m of crushed rock within property boundary.
- Footpath boarded over if protection is required.
- New layback to be formed in a formed kerb if required


LOT 4420

DP: 1313734

425.30m²

LEGEND:

AHD	AUSTRALIAN HEIGHT DATUM
AWN	AWNING
BM	BENCH MARK
CL	CENTRE LINE
CONC	CONCRETE
CS	CONCRETE SURFACE
D/H/S	DIAMETER/HEIGHT/SPREAD
D	DOOR
EC	EDGE OF CONCRETE
EG	EAVE & GUTTER
EP	ELECTRICAL BOX
FL	FLOOR LEVEL
GDN	GARDEN
HYD	HYDRANT
IC	INSPECTION COVER
INV	INVERT LEVEL
KO	KERB OUTLET
LH	LAMP HOLE
LIP	LIP OF KERB
NS	NATURAL SURFACE
PAV	PAVERS
PP	POWER POLE
RL	REDUCED LEVEL
S	STEPS
SL	SURFACE LEVEL
SILL	WINDOW SILL
SIP	SEWER INSPECTION POINT
SMH	SEWER MAN HOLE
SV	STOP VALE
TEL	TELSTRA PIT
TK	TOP OF KERB
TOW/TW	TOP OF WALL
TRW	TOP OF RETAINING WALL
VC	VEHICLE CROSSING
WM	WATER METER
WTOP	TOP OF WINDOW

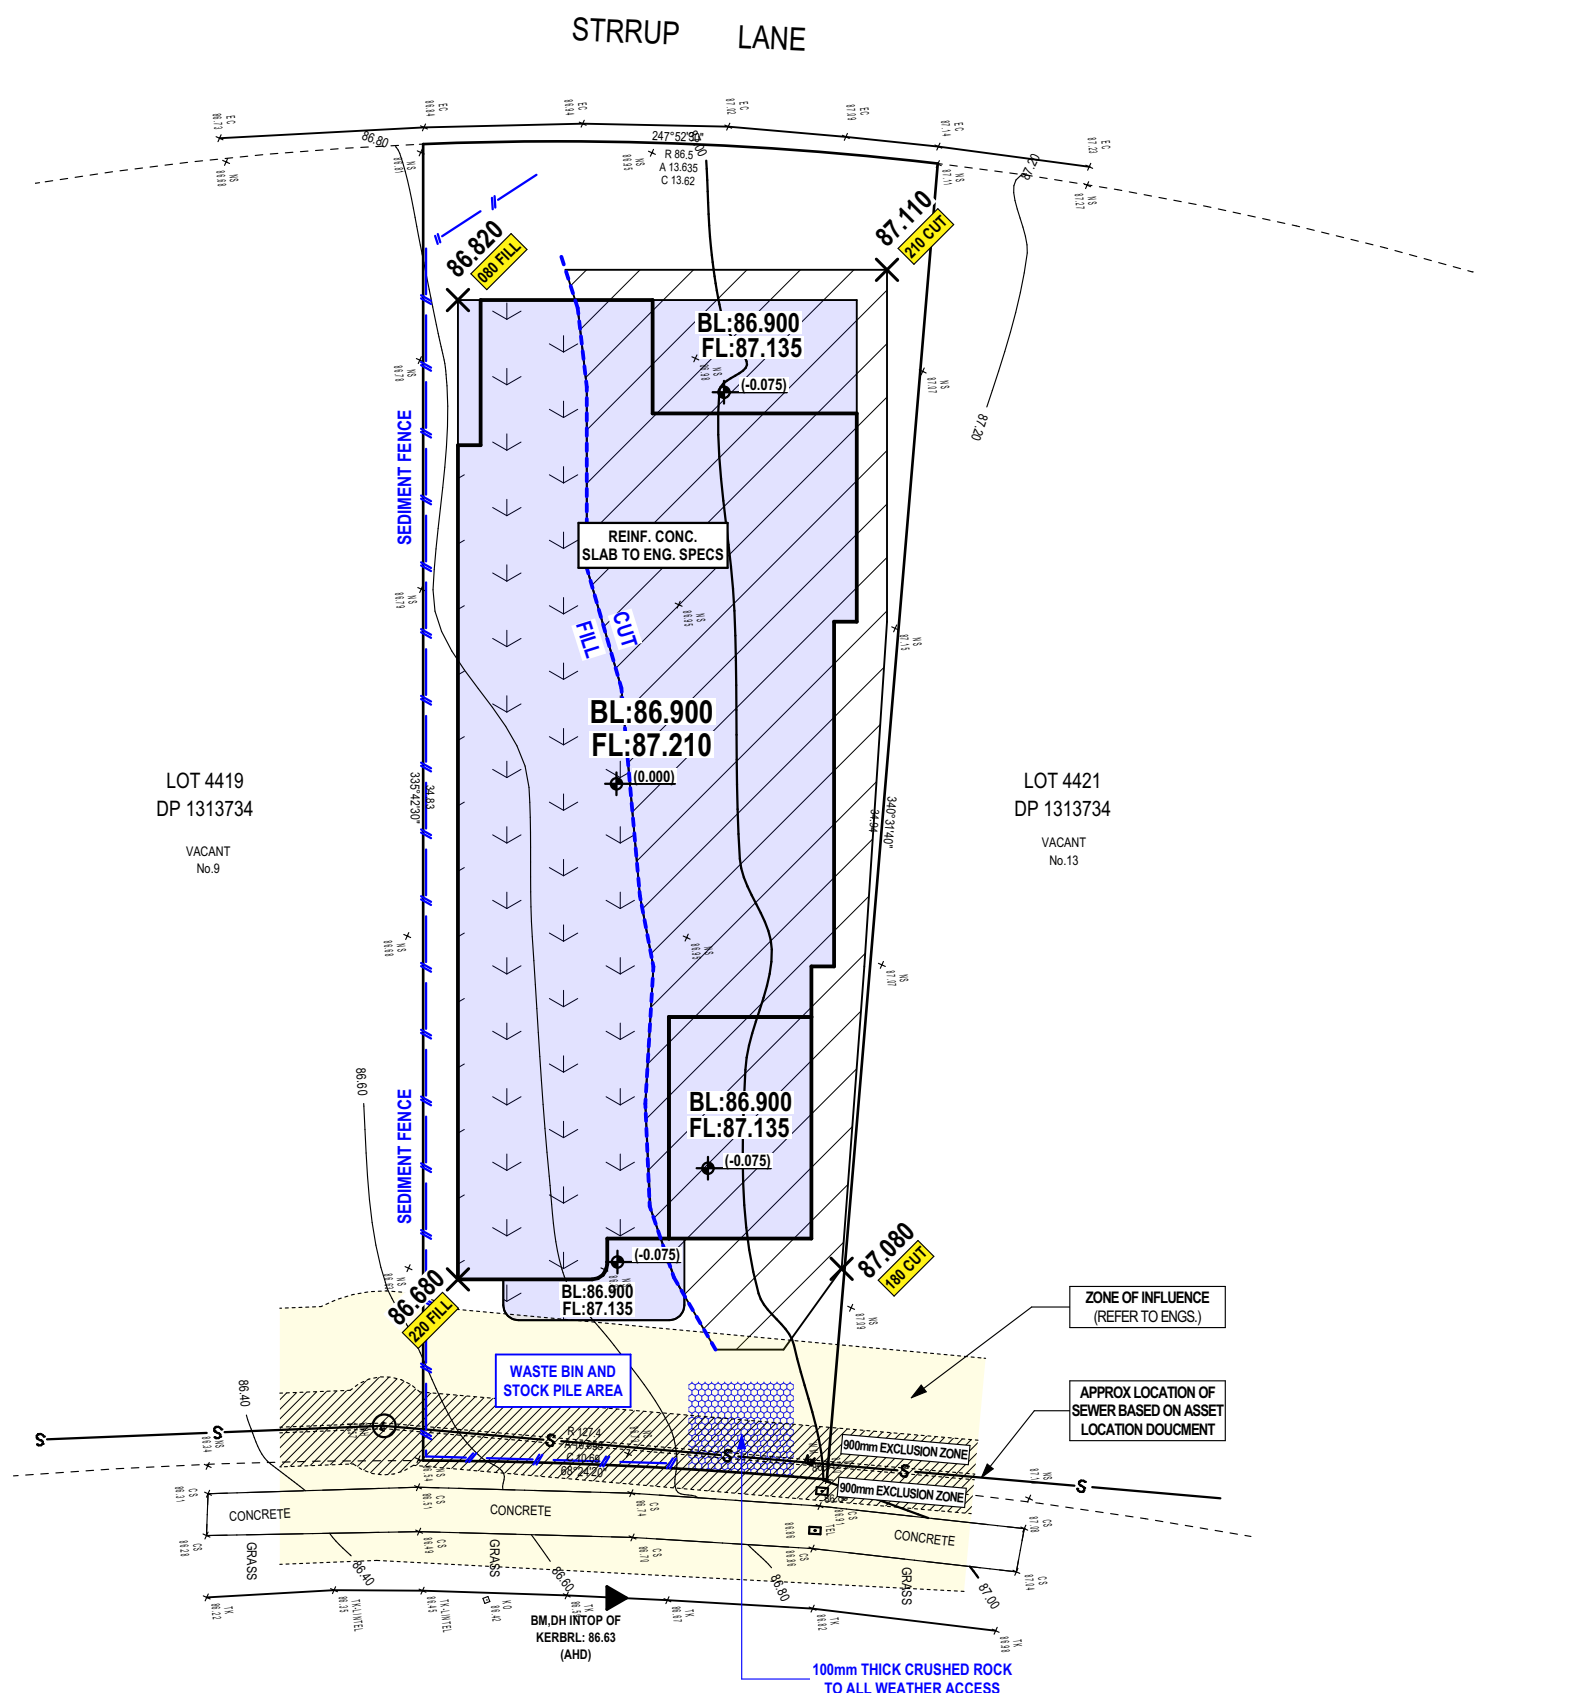

NOTES:

- THIS SURVEY IS SPECIFICALLY FOR CONTOUR PURPOSES ONLY. THE BOUNDARIES OF THE SUBJECT PROPERTY HAVE NOT BEEN INVESTIGATED BY US AND THE POSITION SHOWN IS APPROXIMATE ONLY.
- IF THE DIMENSIONS OR DESCRIPTION OF THE TITLE ARE CRITICAL FOR DESIGN AND/OR CONSTRUCTION OF NEW STRUCTURES OR FINANCIAL DECISIONS WE RECOMMEND THAT AN IDENTIFICATION SURVEY OR RE-SURVEY OF BOUNDARIES BE CARRIED OUT.
- SERVICES SHOWN HAVE BEEN DERIVED FROM VISUAL EVIDENCE APPARENT AT THE TIME OF SURVEY. SERVICES MAY EXIST WHICH ARE NOT SHOWN. THE RELEVANT SERVICE AUTHORITY SHOULD BE CONTACTED TO VERIFY THE EXISTENCE AND POSITION OF SERVICES PRIOR TO THE COMMENCEMENT OF ANY CONSTRUCTION OR EXCAVATION.
- DETAIL ON THIS PLAN HAS BEEN LOCATED FOR PLOTTING PURPOSES ONLY.
- DIAMETER, HEIGHT & SPREAD OF TREES ARE APPROXIMATE ONLY.
- LEVELS SHOWN ARE OF AUSTRALIAN HEIGHT DATUM.
- ORIGIN OF LEVELS: SSM 226792, RL: 88.157(AHD), CLASS LC.
- USE STATED DIMENSIONS. DO NOT SCALE.
- THESE NOTES FORM PART OF THIS PLAN AND CANNOT BE REMOVED. NO COVENANTS AND/OR RESTRICTIONS HAVE BEEN INVESTIGATED BY C & A SURVEYORS PTY LTD.

WALLA WALLA WAY

BCA (NCC) & AUSTRALIAN STANDARDS COMPLIANCE NOTES:

EARTHWORK IS TO COMPLY WITH PART H103 OF NCC 2022 - SITE PREPARATION


TERMITE MANAGEMENT IS TO COMPLY WITH PART H103 OF NCC 2022 - SITE PREPARATION AND AS 3668.1-2014. A DURABLE NOTICE IS TO BE INSTALLED IN ACCORDANCE WITH PART H103 OF NCC 2022, WHERE A CHEMICAL TERMITE MANAGEMENT SYSTEM IS USED, THE CHEMICAL MUST BE INCLUDED ON THE APPROPRIATE AUTHORITY'S PESTICIDES REGISTER

FOOTINGS AND SLABS ARE TO COMPLY WITH AS 2870-2011.


BUSHFIRE BAL-12.5
(In Compliance with AS3959-2018)

FIGURED DIMENSIONS TO BE USED IN PREFERENCE TO SCALING THIS DRAWING
DO NOT ASSUME - IF IN DOUBT ASK.

REF:	DATE:	AMENDMENT:	PROPOSED:	CLIENT:
A	08.07.26	PRELIMINARY PLANS	SINGLE STOREY DWELLING	ELA Projects Pty Ltd
B	23.07.26	DRP AMENDMENTS		
C	21.08.26	CDC PLANS		
			AT: Lot 4420, DP: 1313734 No.11 Walla Walla Way, Menangle Park. NSW 2563	PROJECT FILES JOB NO: 260120 DATE: 08.07.26 DRAWN: MT SHEET SIZE: A2 LGA: Campbelltown City SHEET: 2 of 9


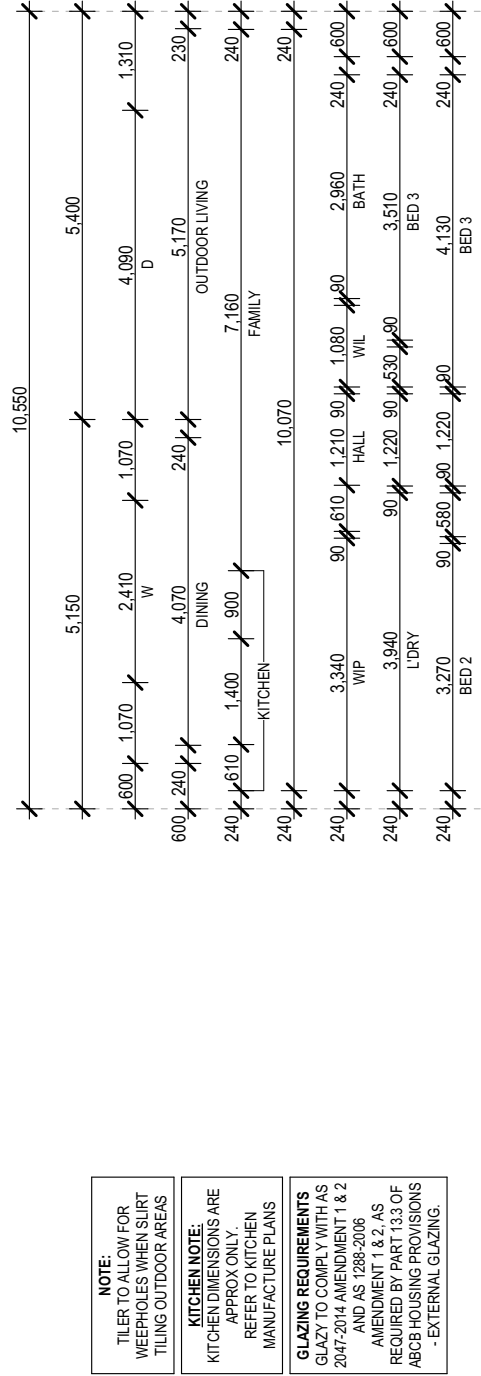


ROOF SPACE VENTILATION:
WIND DRIVEN VENTILATORS &
EAVE VENTS TO BE INSTALLED AS
PER NCC & BASIX REQUIREMENTS

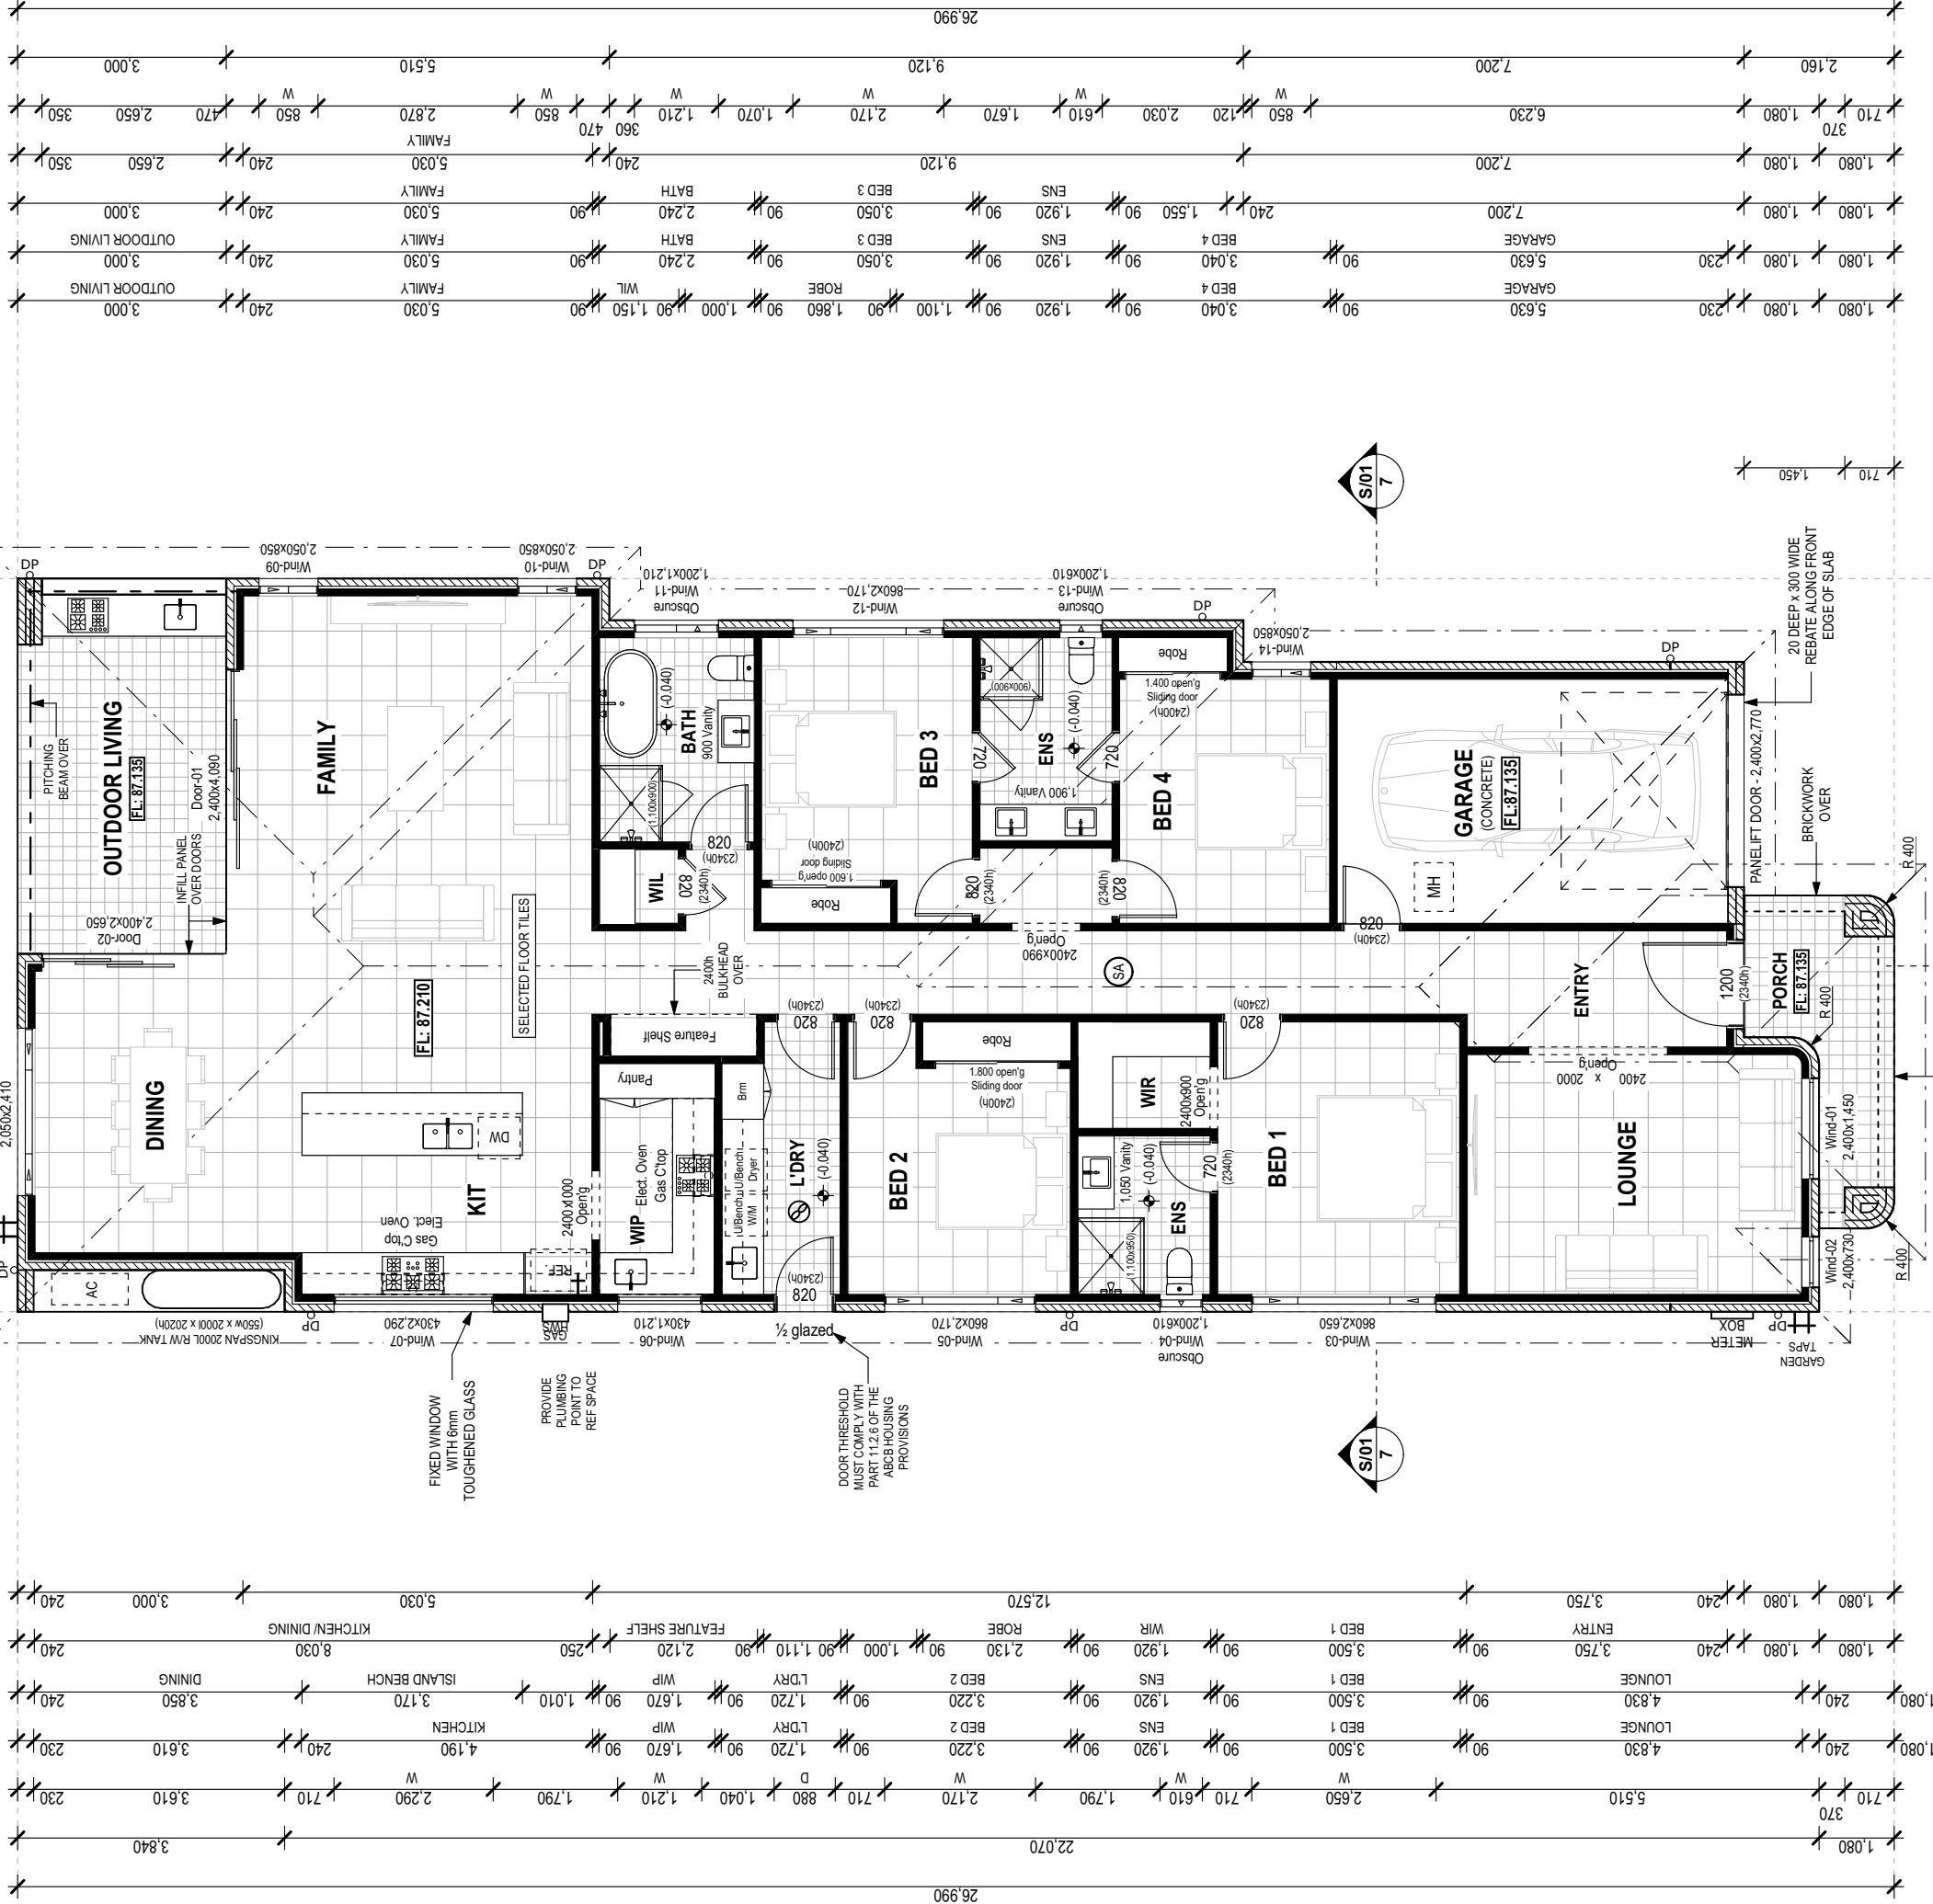


SMOKE ALARM LOCATION
SMOKE ALARMS ARE TO COMPLY WITH
PART 9.5 OF ABC8 HOUSING PROVISIONS -
SMOKE ALARMS AND EVACUATION
LIGHTING AND AS1768:2017 AMENDMENT 1

MECHANICAL VENTILATION
MECHANICAL VENTILATION TO BE
PROVIDED TO LAUNDRY

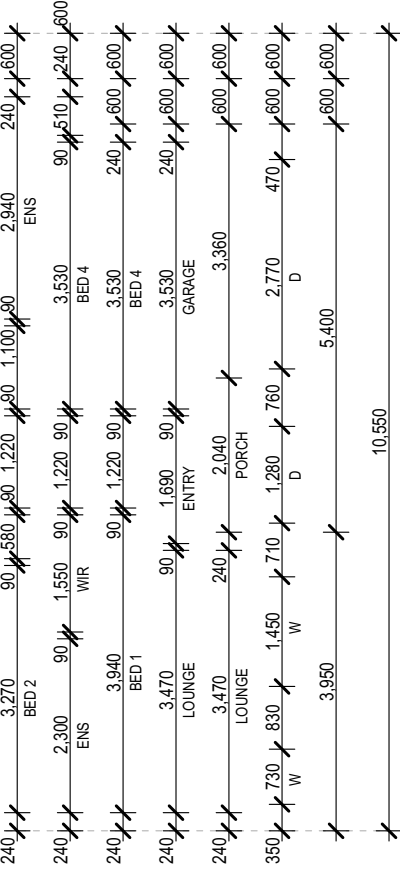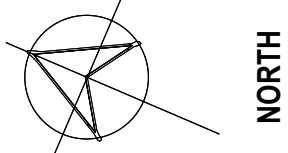

SCALE BAR 1:100

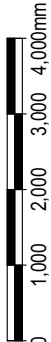

GENERAL NOTES

1. LEVELS SHOWN ARE APPROXIMATE AND TO BE CONFIRMED ON SITE BY SURVEYOR.
2. DIMENSIONS AND LEVELS ARE REQUIRED AND THOSE DRAWINGS SHOWN ARE TO BE USED TO BEST ADVANTAGE.
3. ALL BOUNDARY CLEARANCES MUST BE VERIFIED BEFORE COMMENCEMENT OF BUILDING WORKS BY REGISTERED SURVEYOR.
4. OF BUILDING WORKS BY REGISTERED SURVEYOR.
5. IN CASE OF ALTERATIONS OR DISCREPANCIES AND AUSTRALIAN STANDARDS. NOTIFY TAYLORED DESIGNS & DRAFTING IMMEDIATELY.

REF: DATE: AMENDMENT:

REF:	DATE:	AMENDMENT:
A	08.07.26	PRELIMINARY PLANS
B	23.07.26	DRP AMENDMENTS
C	21.08.26	DDC PLANS

PROPOSED: SINGLE STOREY DWELLING


AT:	Lot: 4420, DP: 1313734
	No.11 Walla Walla Way,
	Menangle Park. NSW 2563

PROJECT FILES

CLIENT:


ELA Projects Pty Ltd



JOB NO:	260120	DATE:	08.07.26	DRAWN:	MT
Sheet Size:	A2	LGA:	Campbelltown City	Sheet:	3 of 9

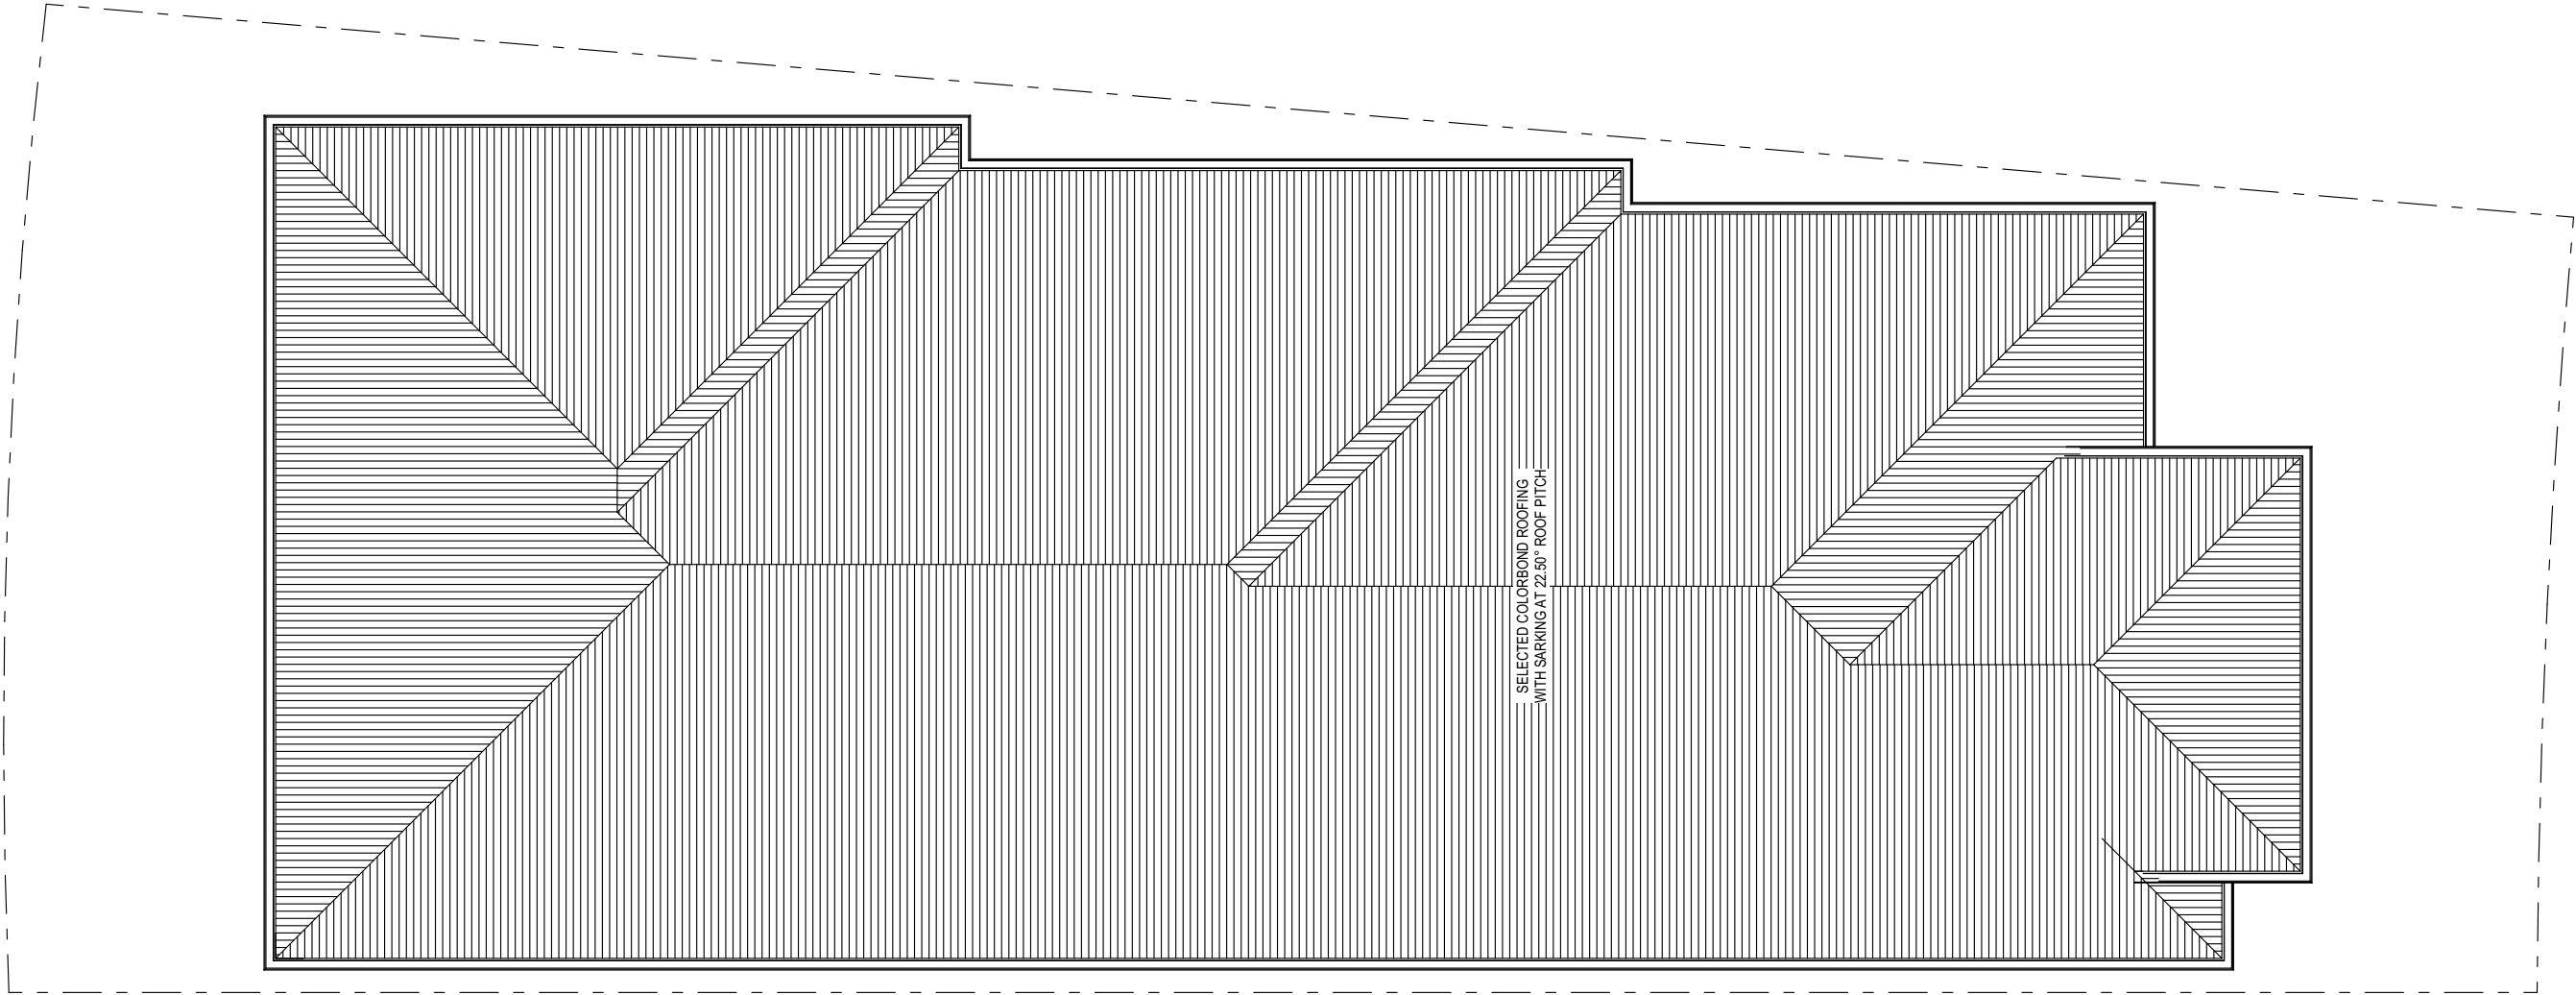


ROOF SPACE VENTILATION:
WIND DRIVEN VENTILATORS &
EAVES VENTILATORS TO BE
INSTALLED PER NCC & BASIX REQUIREMENTS

ROOF AREA (m2)	
Pitch	Horizontal Area
22.50°	295.35

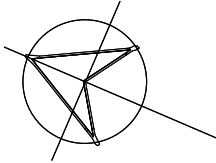

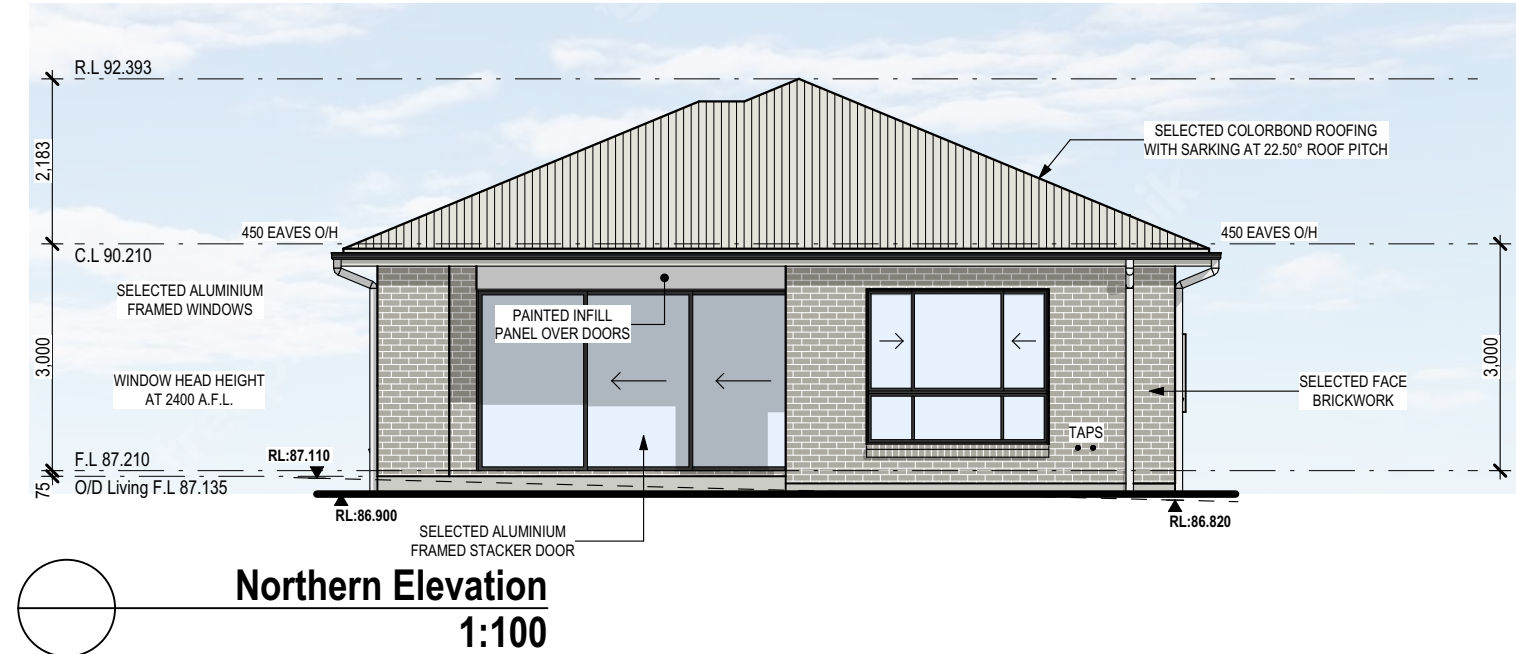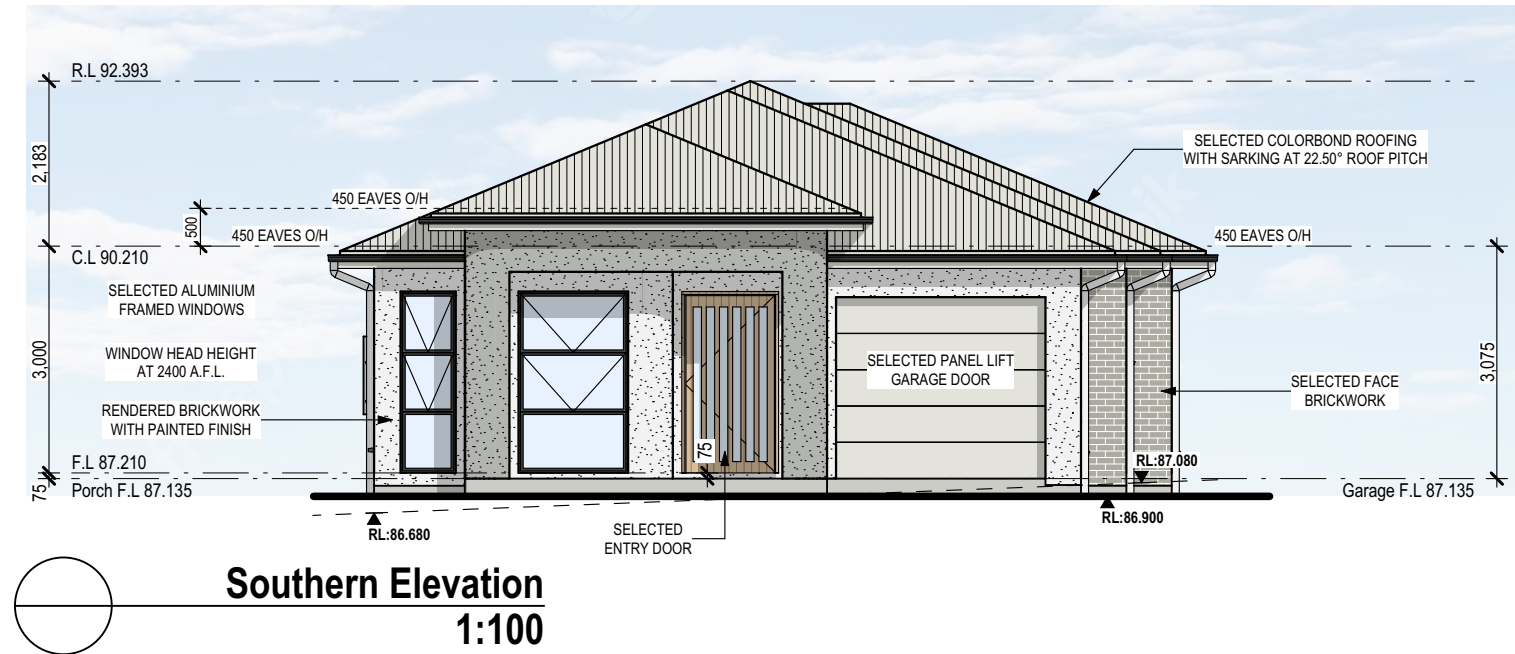

Window / Door Schedule					
ID	Plan Symbol	Type	Glazing Type	Height	Width
Door-01		ALUMINIUM STACKER	CLEAR	2,400	4,278
Door-02		ALUMINIUM STACKER	CLEAR	2,400	2,838
Wind-01		ALUMINIUM AWNING	CLEAR	2,400	1,450
Wind-02		ALUMINIUM AWNING	CLEAR	2,400	730
Wind-03		ALUMINIUM SLIDING	CLEAR	860	2,650
Wind-04		ALUMINIUM AWNING	OBSCURE	1,200	610
Wind-05		ALUMINIUM SLIDING	CLEAR	860	2,170
Wind-06		ALUMINIUM FIXED	CLEAR	430	1,210
Wind-07		ALUMINIUM FIXED	CLEAR	430	2,290
Wind-08		ALUMINIUM SLIDING	CLEAR	2,050	2,410
Wind-09		ALUMINIUM SLIDING	CLEAR	2,050	850
Wind-10		ALUMINIUM SLIDING	CLEAR	2,050	850
Wind-11		ALUMINIUM AWNING	OBSCURE	1,200	1,210
Wind-12		ALUMINIUM SLIDING	CLEAR	860	2,170
Wind-13		ALUMINIUM AWNING	OBSCURE	1,200	610
Wind-14		ALUMINIUM SLIDING	CLEAR	2,050	850

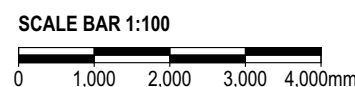

TAYLORED
DESIGNS & DRAFTING

Phone: 0401 482 401 Email: info@tayloredesigns.com.au

Copyright. © This plan is the property of Taylored Designs & Drafting and may not be used in whole or part

- GENERAL NOTES**
- LEVELS SHOWN ARE APPROXIMATE AND TO BE CONFIRMED ON SITE BY SURVEYOR.
 - ENGINEERS DRAWINGS ARE REQUIRED AND THOSE DRAWINGS MUST TAKE PREFERENCE TO THESE DRAWINGS
 - ALL BOUNDARY CLEARANCES MUST BE VERIFIED BEFORE COMMENCEMENT OF BUILDING WORKS BY REGISTERED SURVEYOR.
 - BUILDER IS TO STRICTLY COMPLY WITH ALL RELEVANT BUILDING CODE OF AUSTRALIA CONSTRUCTION REQUIREMENTS AND AUSTRALIAN STANDARDS.
 - IN CASE OF ALTERATIONS OR DISCREPANCIES NOTIFY TAYLORED DESIGNS & DRAFTING IMMEDIATELY.

REF:	DATE:	AMENDMENT:
A	08.07.26	PRELIMINARY PLANS
B	23.07.26	DRP AMENDMENTS
C	21.08.26	CDC PLANS

PROPOSED: SINGLE STOREY DWELLING

AT: Lot: 4420, DP: 1313734
No.11 Walla Walla Way,
Menangle Park. NSW 2563

CLIENT: ELA Projects Pty Ltd

PROJECT FILES


JOB NO: 260120 **DATE:** 08.07.26 **DRAWN:** MT

Sheet Size: A2 **LGA:** Campbelltown City **Sheet:** 5 of 9


FIGURED DIMENSIONS TO BE USED IN PREFERENCE TO SCALING THIS DRAWING DO NOT ASSUME - IF IN DOUBT ASK.

bdca ACCREDITED BUILDING DESIGNER


BUSHFIRE BAL-12.5
(In Compliance with AS3959-2018)

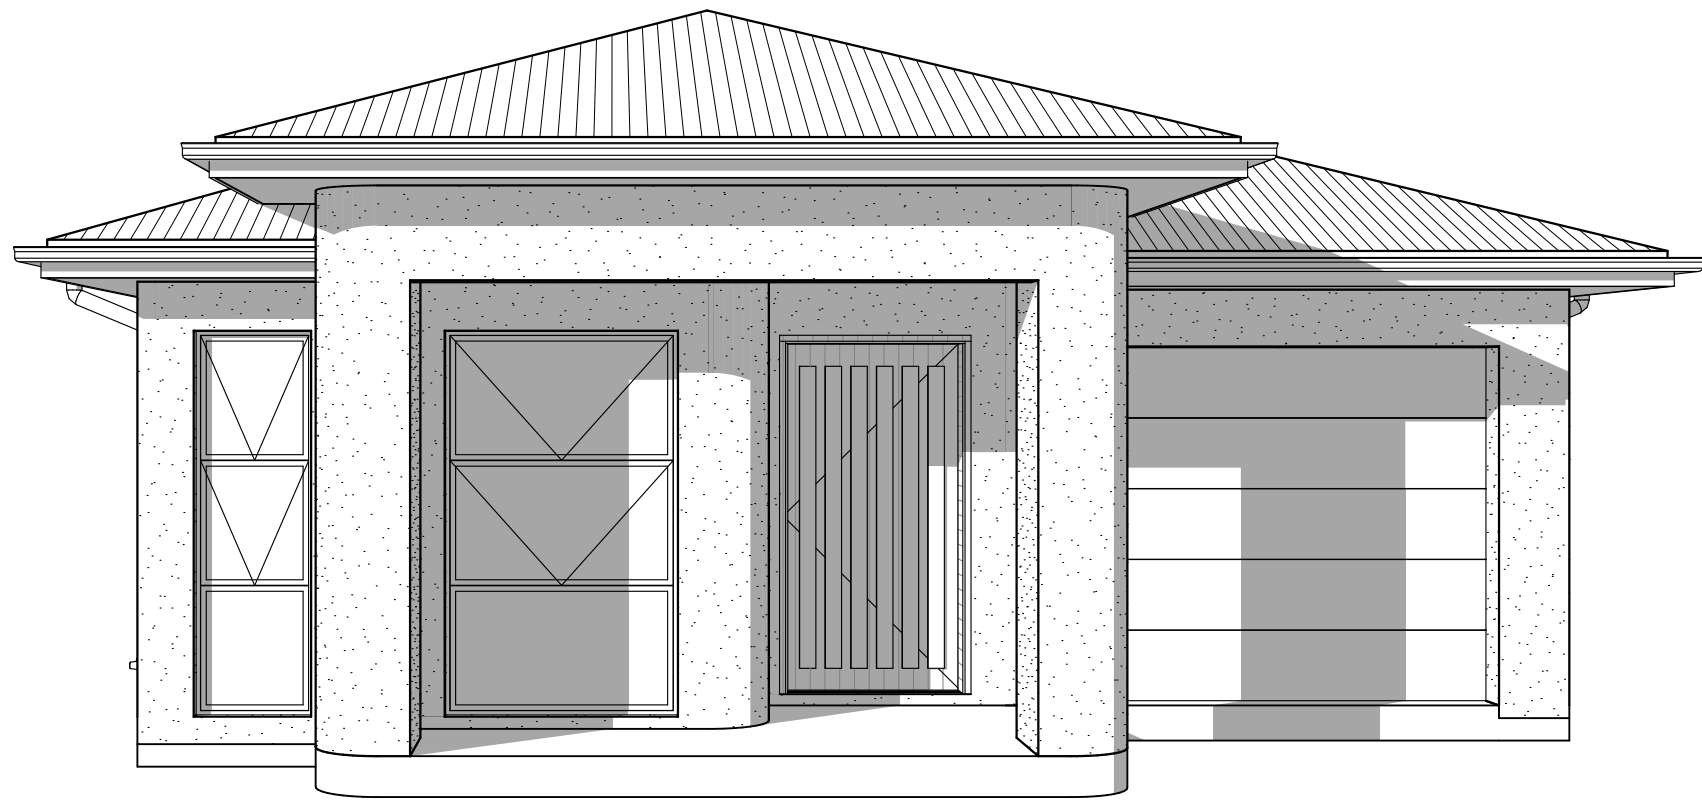

Front Perspective 01

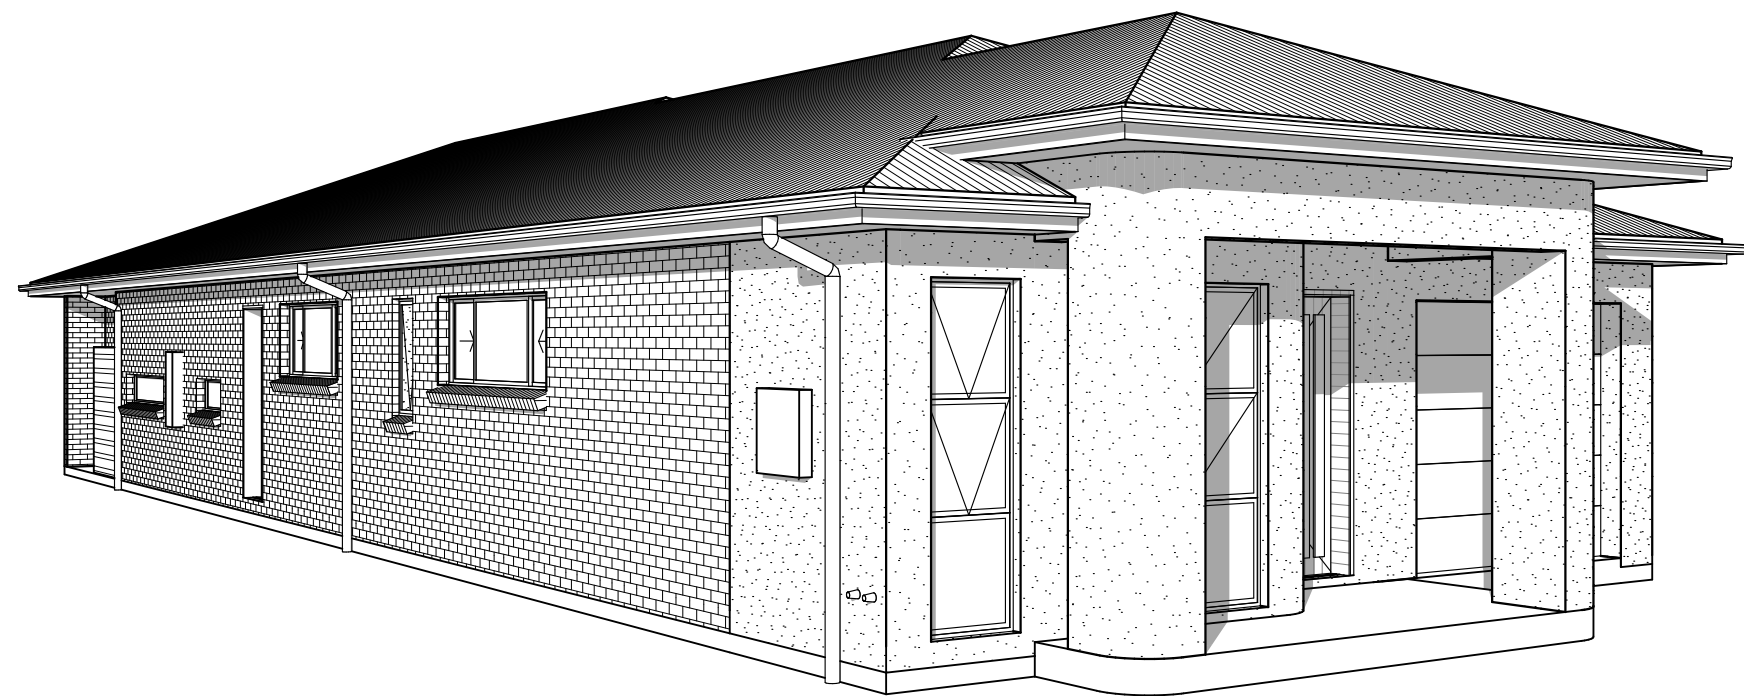

Front Perspective 02

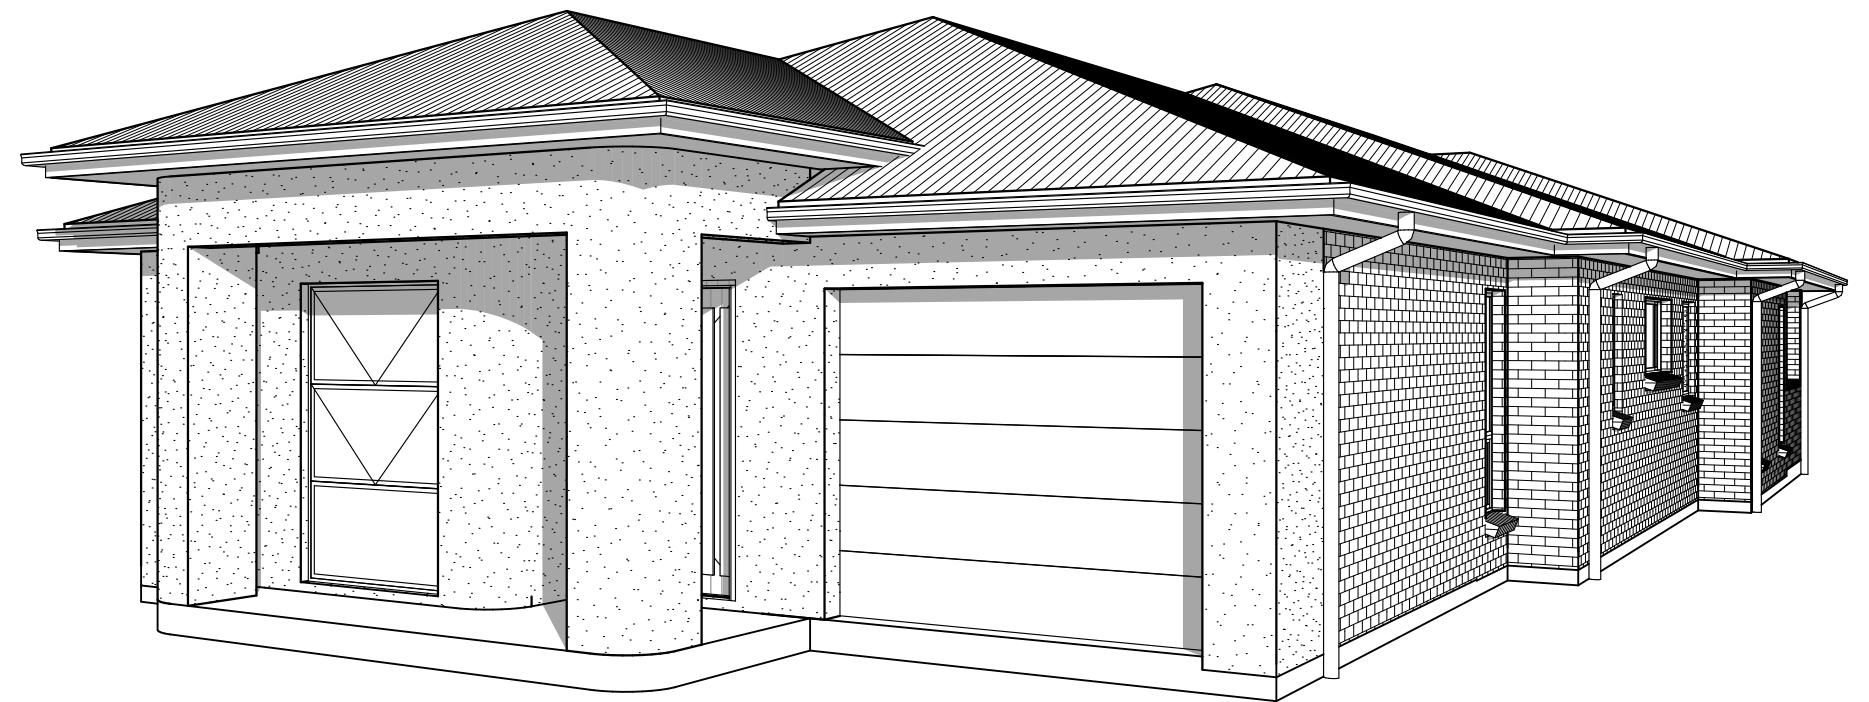

Front Perspective 03

FIGURED DIMENSIONS TO BE USED IN
PREFERENCE TO SCALING THIS DRAWING
DO NOT ASSUME - IF IN DOUBT ASK.



BUSHFIRE BAL-12.5
(In Compliance with AS3959-2018)



TAYLORED
DESIGNS & DRAFTING

Phone: 0401 482 401 Email: info@taylorreddesigns.com.au

Copyright. © This plan is the property of Taylorred Designs & Drafting and may not be used in whole or part

GENERAL NOTES

- LEVELS SHOWN ARE APPROXIMATE AND TO BE CONFIRMED ON SITE BY SURVEYOR.
- ENGINEERS DRAWINGS ARE REQUIRED AND THOSE DRAWINGS MUST TAKE PREFERENCE TO THESE DRAWINGS
- ALL BOUNDARY CLEARANCES MUST BE VERIFIED BEFORE COMMENCEMENT OF BUILDING WORKS BY REGISTERED SURVEYOR.
- BUILDER IS TO STRICTLY COMPLY WITH ALL RELEVANT BUILDING CODE OF AUSTRALIA CONSTRUCTION REQUIREMENTS AND AUSTRALIAN STANDARDS.
- IN CASE OF ALTERATIONS OR DISCREPANCIES NOTIFY TAYLORED DESIGNS & DRAFTING IMMEDIATELY.

REF:	DATE:	AMENDMENT:
A	08.07.26	PRELIMINARY PLANS
B	23.07.26	DRP AMENDMENTS
C	21.08.26	CDC PLANS





PROPOSED: SINGLE STOREY DWELLING

AT: Lot: 4420, DP: 1313734
No.11 Walla Walla Way,
Menangle Park. NSW 2563


CLIENT:
ELA Projects Pty Ltd




JOB NO: 260120	DATE: 08.07.26	DRAWN: MT
Sheet Size: A2	LGA: Campbelltown City	Sheet: 6 of 9

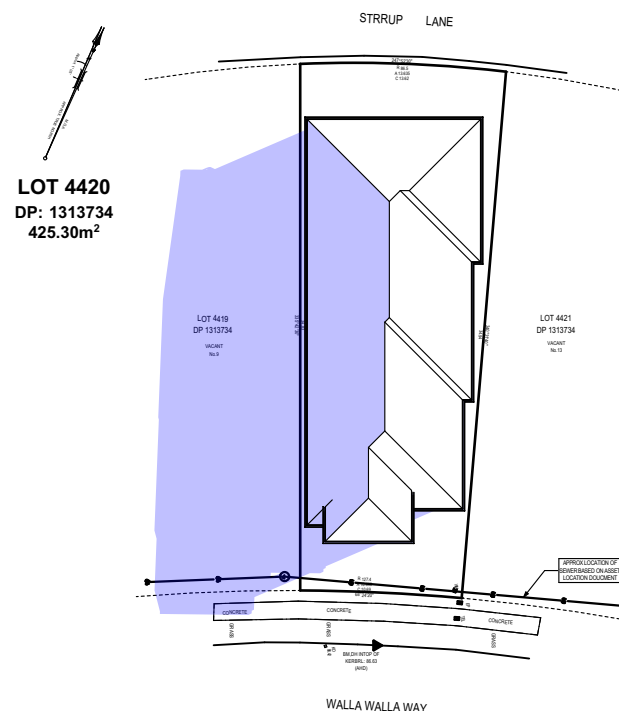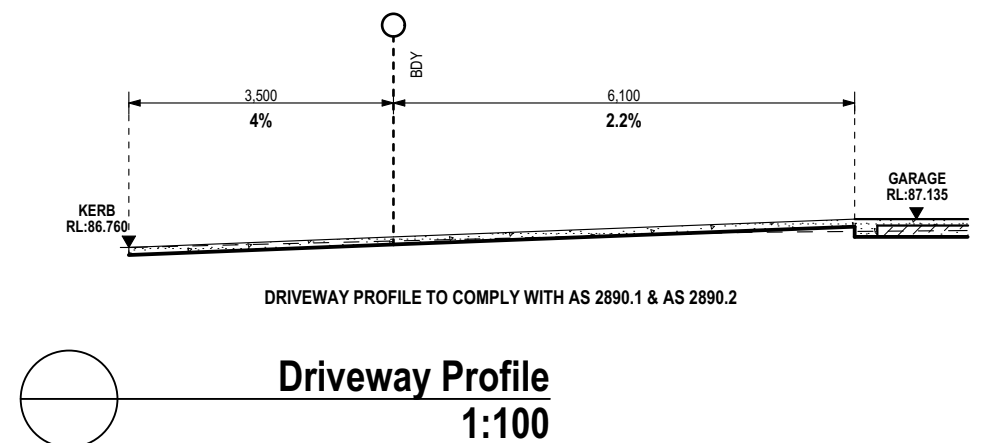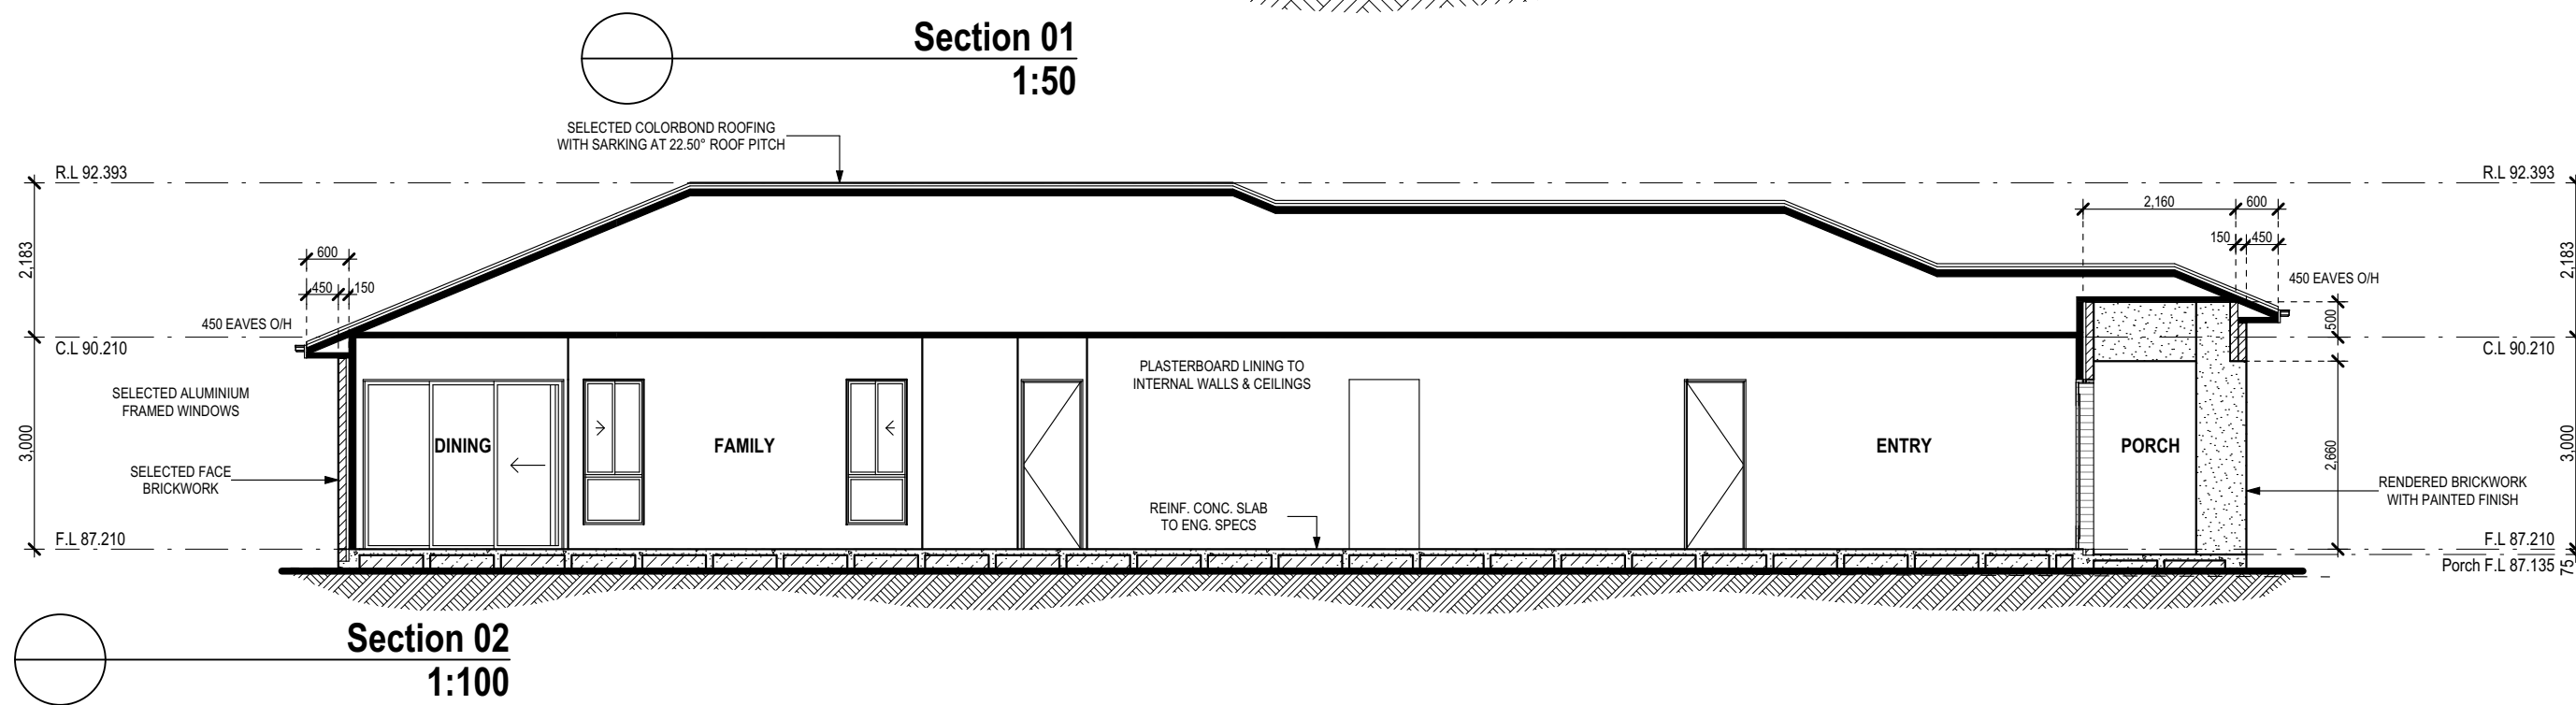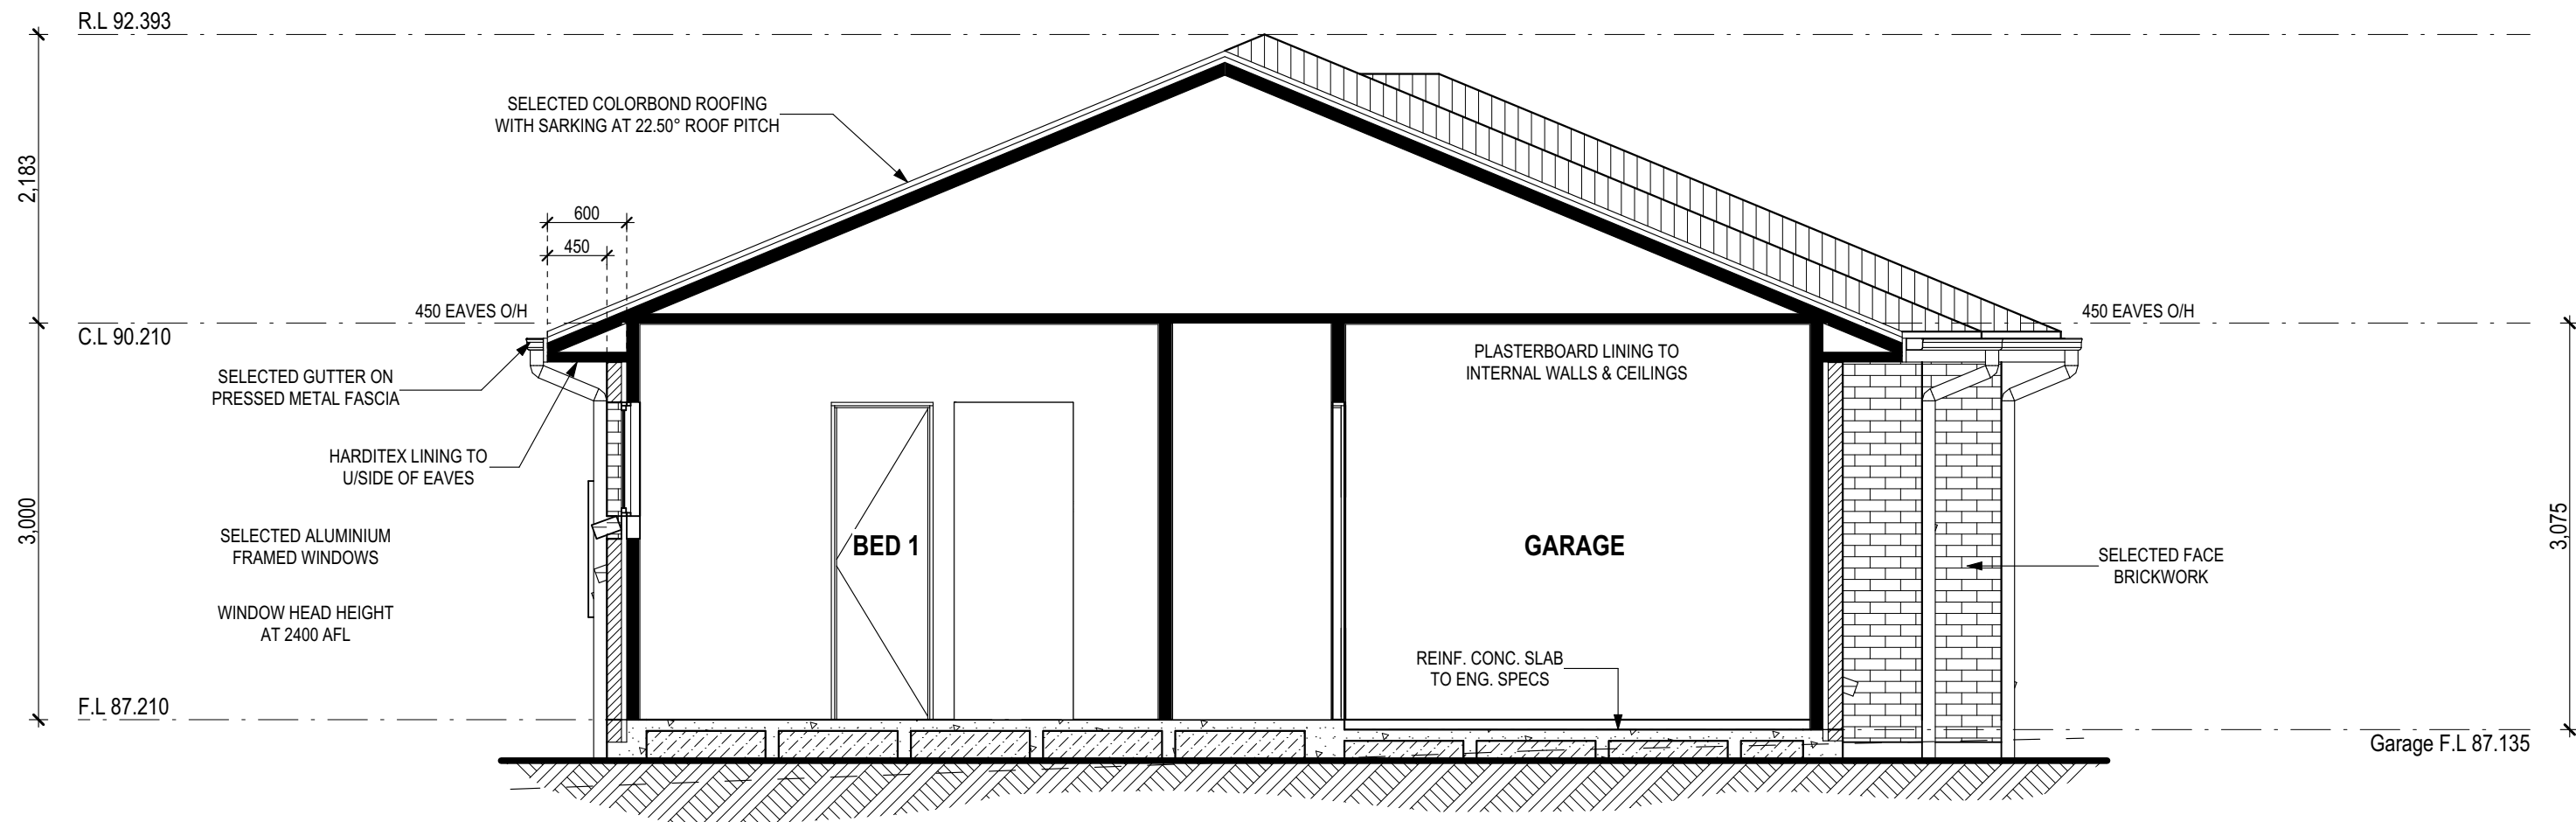



June 21st- 9am
1:500

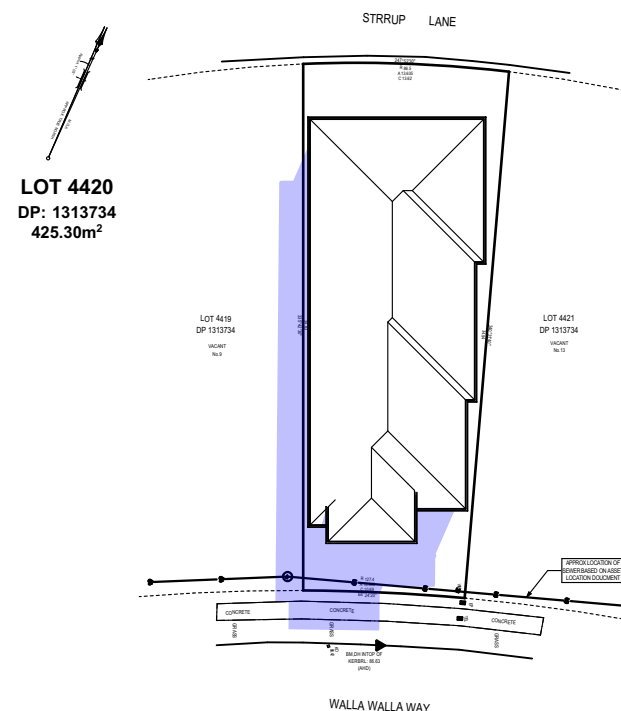

June 21st- 12pm
1:500

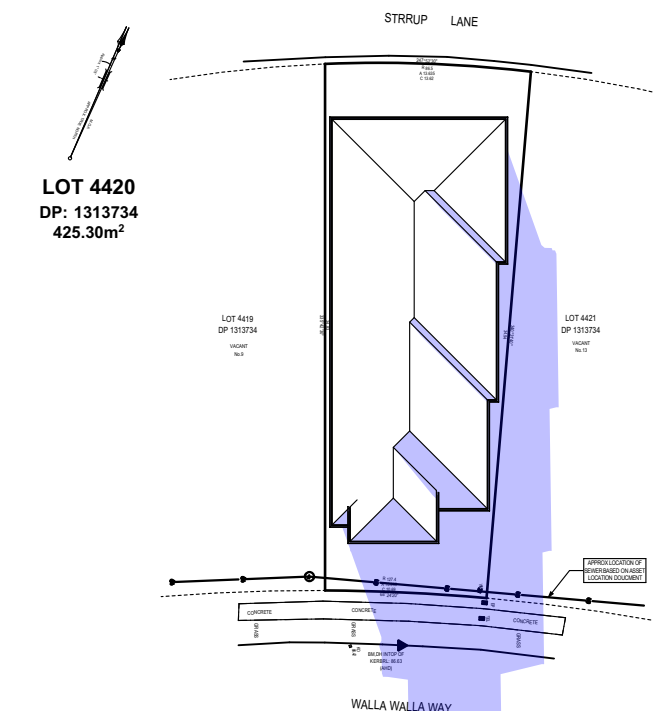


June 21st- 3pm
1:500

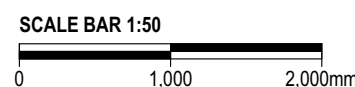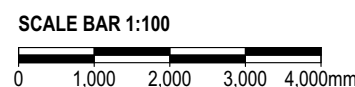

FIGURED DIMENSIONS TO BE USED IN PREFERENCE TO SCALING THIS DRAWING DO NOT ASSUME - IF IN DOUBT ASK.



BUSHFIRE BAL-12.5
(In Compliance with AS3959-2018)

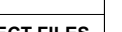 TAYLORED DESIGNS & DRAFTING Phone: 0401 482 401 Email: info@taylorreddesigns.com.au Copyright. © This plan is the property of Taylorred Designs & Drafting and may not be used in whole or part		<u>GENERAL NOTES</u>		<table><tr><th>REF:</th><th>DATE:</th><th>AMENDMENT:</th></tr><tr><td>A</td><td>08.07.26</td><td>PRELIMINARY PLANS</td></tr><tr><td>B</td><td>23.07.26</td><td>DRP AMENDMENTS</td></tr><tr><td>C</td><td>21.08.26</td><td>CDC PLANS</td></tr></table>		REF:	DATE:	AMENDMENT:	A	08.07.26	PRELIMINARY PLANS	B	23.07.26	DRP AMENDMENTS	C	21.08.26	CDC PLANS	PROPOSED: SINGLE STOREY DWELLING		CLIENT:	
		REF:	DATE:	AMENDMENT:																	
		A	08.07.26	PRELIMINARY PLANS																	
		B	23.07.26	DRP AMENDMENTS																	
C	21.08.26	CDC PLANS																			
		1. LEVELS SHOWN ARE APPROXIMATE AND TO BE CONFIRMED ON SITE BY SURVEYOR. 2. ENGINEERS DRAWINGS ARE REQUIRED AND THOSE DRAWINGS MUST TAKE PREFERENCE TO THESE DRAWINGS. 3. ALL BOUNDARY CLEARANCES MUST BE VERIFIED BEFORE COMMENCEMENT OF BUILDING WORKS BY REGISTERED SURVEYOR. 4. BUILDER IS TO STRICTLY COMPLY WITH ALL RELEVANT BUILDING CODE OF AUSTRALIA CONSTRUCTION REQUIREMENTS AND AUSTRALIAN STANDARDS. 5. IN CASE OF ALTERATIONS OR DISCREPANCIES NOTIFY TAYLORED DESIGNS & DRAFTING IMMEDIATELY.		AT: Lot: 4420, DP: 1313734 No.11 Walla Walla Way, Menangle Park. NSW 2563		ELA Projects Pty Ltd															
						 PROJECT FILES															
						<table><tr><td>JOB NO:</td><td>DATE:</td><td>DRAWN:</td></tr><tr><td>260120</td><td>08.07.26</td><td>MT</td></tr><tr><td>Sheet Size:</td><td>LGA:</td><td>Sheet:</td></tr><tr><td>A2</td><td>Campbelltown City</td><td>7 of 9</td></tr></table>		JOB NO:	DATE:	DRAWN:	260120	08.07.26	MT	Sheet Size:	LGA:	Sheet:	A2	Campbelltown City	7 of 9		
JOB NO:	DATE:	DRAWN:																			
260120	08.07.26	MT																			
Sheet Size:	LGA:	Sheet:																			
A2	Campbelltown City	7 of 9																			

BASIX™Certificate

Building Sustainability Index
www.planningportal.nsw.gov.au/development-and-assessment/basix

Single Dwelling

Certificate number: 1862104S

This certificate confirms that the proposed development will meet the NSW government's requirements for sustainability, if it is built in accordance with the commitments set out below. Terms used in this certificate, or in the commitments, have the meaning given by the document entitled "BASIX Definitions" dated 10/09/2020 published by the Department. This document is available at www.planningportal.nsw.gov.au/definitions

Secretary
Date of issue: Friday, 21 August 2026
To be valid, this certificate must be submitted with a development application or lodged with a complying development certificate application within 3 months of the date of issue.



Project summary		
Project name	Dwelling @ 11 Walla Walla Way, Menangle Park	
Street address	11 WALLA WALLA Way MENANGLE PARK 2563	
Local Government Area	Campbelltown City Council	
Plan type and plan number	Deposited Plan DP1313734	
Lot no.	4420	
Section no.	-	
Project type	dwelling house (detached)	
No. of bedrooms	4	
Project score		
Water	✔ 40	Target 40
Thermal Performance (Do-it-Yourself Method)	✔ Pass	Target Pass
Energy	✔ 71	Target 70
Materials	✔ -55	Target n/a

WATER:				
Fixtures	All Shower Heads:	All Toilet Flushing Systems:	All Kitchen Taps:	All Bathroom Taps:
	4 star (> 6 but <= 7.5 L/min)	4 Star	4 Star	4 Star
Alternative water source	Rainwater tank size min - 2000 litres Rainwater tank to collect run off from at least 90m² of roof area			
	Landscape connection:	Toilet connection:	Laundry connection:	Pool top up:
	Yes	Yes	No	NA
ENERGY:				
Hot water system: Gas Instantaneous with a performance of 6 stars				
Bathroom ventilation system: Individual fan, ducted to façade or roof; manual switch on/off				
Kitchen ventilation system: Individual fan, ducted to façade or roof; manual switch on/off				
Laundry ventilation system: Individual fan, ducted to façade or roof; manual switch on/off				
Cooling system: 1 Phase air-conditioning (3 Star) in at least 1 living/bed area (zoned)				
Heating system: 1 Phase air-conditioning (3 Star) in at least 1 living/bed area (zoned)				
Natural lighting: As per BASIX Certificate				
Artificial lighting: As per BASIX Certificate				
Alternative energy: NA				
Must install a gas cooktop and electric oven.				
Must install fixed outdoor clothes drying line as part of the development.				

Thermal Performance and Materials commitments	Show on DA plans	Show on CC/CDC plans & specs	Certifier check
Do-it-yourself Method			
General features			
The dwelling must be a Class 1 dwelling according to the National Construction Code, and must not have more than 2 storeys.	✔	✔	✔
The conditioned floor area of the dwelling must not exceed 300 square metres.	✔	✔	✔
The dwelling must not contain open mezzanine area exceeding 25 square metres.	✔	✔	✔
The dwelling must not contain third level habitable attic room.	✔	✔	✔
Floor, walls and ceiling/roof			
The applicant must construct the floor(s), walls, and ceiling/roof of the dwelling in accordance with the specifications listed in the table below.	✔	✔	✔
The applicant must adopt one of the options listed in the tables below to address thermal bridging in metal framed floor(s), walls and ceiling/roof of the dwelling.	✔	✔	✔
The applicant must show through receipts that the materials purchased for construction are consistent with the specifications listed in the tables below.			✔

Construction	Area - m²	Additional insulation required	Options to address thermal bridging	Other specifications
floor - concrete slab on ground, waffle pod slab.	193	nil;not specified	nil	
garage floor - concrete slab on ground, waffle pod slab.	20	none	nil	
external wall: brick veneer; frame: timber - untreated softwood.	all external walls	2.94 (or 3.50 including construction);fibreglass batts or roll	nil	wall colour: Medium (solar absorptance 0.48-0.7)
external garage wall: brick veneer; frame: timber - untreated softwood.	19	fibreglass batts or roll	nil	
internal wall shared with garage: plasterboard; frame: timber - untreated softwood.	22	nil;none	nil	
internal wall: plasterboard; frame: timber - untreated softwood.	175	none	nil	
ceiling and roof - flat ceiling / pitched roof, framed - metal roof, timber - untreated softwood.	294	ceiling: 5 (up), roof: foil backed blanket ;ceiling: fibreglass batts or roll; roof: foil backed blanket.	nil	roof space ventilation: wind-driven ventilator(s) + eave vents; roof colour: medium (solar absorptance 0.48-0.59); 0.5 to ≤ 1.0% of ceiling area uninsulated

Note	• Insulation specified in this Certificate must be installed in accordance with the ABCB Housing Provisions (Part 13.2.2) of the National Construction Code.
Note	• If the additional ceiling insulation listed in the table above is greater than R3.0, refer to the ABCB Housing Provisions (Part 13.2.3 (6)) of the National Construction Code.
Note	• In some climate zones, insulation should be installed with due consideration of condensation and associated interaction with adjoining building materials.
Note	• Thermal breaks must be installed in metal framed walls and applicable roofs in accordance with the ABCB Housing Provisions of the National Construction Code.

Thermal Performance and Materials commitments	Show on DA plans	Show on CC/CDC plans & specs	Certifier check
Ceiling fans			
The applicant must install at least one ceiling fan in at least one daytime habitable space, such as living room.	✔	✔	✔
• The minimum number and diameter of ceiling fans in a daytime habitable space must be installed in accordance with the ABCB Housing Provisions (Part 13.5.2) of the National Construction Code .	✔	✔	✔

Thermal Performance and Materials commitments	Show on DA plans	Show on CC/CDC plans & specs	Certifier check
Glazed windows, doors and skylights			
The applicant must install the windows, glazed doors and shading devices described in the table below, in accordance with the specifications listed in the table. Relevant overshadowing specifications must be satisfied for each glazed window and door.	✔	✔	✔
The dwelling may have 1 skylight (<0.7 square metres) which is not listed in the table.	✔	✔	✔
The following requirements must also be satisfied in relation to each window and glazed door:	✔	✔	✔
• The applicant must install windows and glazed doors in accordance with the height and width, frame and glazing types listed in the table.	✔	✔	✔
• Each window and glazed door must have a U-value no greater than that listed and a Solar Heat Gain Coefficient (SHGC) within the range listed. Total system U values and SHGC must be calculated in accordance with National Fenestration Rating Council (NFRC) conditions.		✔	✔
The applicant must install the skylights described in the table below, in accordance with the specifications listed in the table. Total skylight area must not exceed 3 square metres (the 3 square metre limit does not include the optional additional skylight of less than 0.7 square metres that does not have to be listed in the table).	✔	✔	✔

Glazed window/door no.	Maximum height (mm)	Maximum width (mm)	Frame and glass specification	Shading device (Dimension within 10%)	Overshadowing
North facing					
W08	2050.00	2410.00	aluminium, single glazed (U-value: <=6.5, SHGC: 0.74 - 0.90)	eave 450 mm, 305 mm above head of window or glazed door	not overshadowed
D01	2400.00	4278.00	aluminium, single glazed (U-value: <=6.5, SHGC: 0.74 - 0.90)	solid overhang 3450 mm, 305 mm above head of window or glazed door	not overshadowed
East facing					
W09	2050.00	850.00	aluminium, single glazed (U-value: <=6.5, SHGC: 0.74 - 0.90)	eave 450 mm, 305 mm above head of window or glazed door	not overshadowed
W10	2050.00	850.00	aluminium, single glazed (U-value: <=6.5, SHGC: 0.74 - 0.90)	eave 450 mm, 305 mm above head of window or glazed door	not overshadowed
W11	1200.00	1210.00	aluminium, single glazed (U-value: <=6.5, SHGC: 0.74 - 0.90)	eave 450 mm, 305 mm above head of window or glazed door	not overshadowed
W12	860.00	2170.00	aluminium, single glazed (U-value: <=6.5, SHGC: 0.74 - 0.90)	eave 450 mm, 305 mm above head of window or glazed door	not overshadowed
W13	1200.00	610.00	aluminium, single glazed (U-value: <=6.5, SHGC: 0.74 - 0.90)	eave 450 mm, 305 mm above head of window or glazed door	not overshadowed
W14	2050.00	850.00	aluminium, single glazed (U-value: <=6.5, SHGC: 0.74 - 0.90)	eave 450 mm, 305 mm above head of window or glazed door	not overshadowed
D02	2400.00	2838.00	aluminium, single glazed (U-value: <=6.5, SHGC: 0.74 - 0.90)	solid overhang 5850 mm, 305 mm above head of window or glazed door	not overshadowed
South facing					
W01	2400.00	1450.00	aluminium, single glazed (U-value: <=6.5, SHGC: 0.74 - 0.90)	solid overhang 1530 mm, 260 mm above head of window or glazed door	not overshadowed
W02	2400.00	730.00	aluminium, single glazed (U-value: <=6.5, SHGC: 0.74 - 0.90)	eave 450 mm, 320 mm above head of window or glazed door	not overshadowed
West facing					
W03	860.00	2650.00	aluminium, single glazed (U-value: <=6.5, SHGC: 0.74 - 0.90)	eave 450 mm, 305 mm above head of window or glazed door	not overshadowed
W04	1200.00	610.00	aluminium, single glazed (U-value: <=6.5, SHGC: 0.74 - 0.90)	eave 450 mm, 305 mm above head of window or glazed door	not overshadowed
W05	860.00	2170.00	aluminium, single glazed (U-value: <=6.5, SHGC: 0.74 - 0.90)	eave 450 mm, 305 mm above head of window or glazed door	not overshadowed
W06	430.00	1210.00	aluminium, single glazed (U-value: <=6.5, SHGC: 0.74 - 0.90)	eave 450 mm, 1250 mm above head of window or glazed door	not overshadowed
W07	430.00	2290.00	aluminium, single glazed (U-value: <=6.5, SHGC: 0.74 - 0.90)	eave 450 mm, 1250 mm above head of window or glazed door	not overshadowed

FIGURED DIMENSIONS TO BE USED IN PREFERENCE TO SCALING THIS DRAWING
DO NOT ASSUME - IF IN DOUBT ASK.



BUSHFIRE BAL-12.5
(In Compliance with AS3959-2018)

 TAYLORED DESIGNS & DRAFTING Phone: 0401 482 401 Email: info@taylorreddesigns.com.au Copyright. © This plan is the property of Taylored Designs & Drafting and may not be used in whole or part	GENERAL NOTES 1. LEVELS SHOWN ARE APPROXIMATE AND TO BE CONFIRMED ON SITE BY SURVEYOR. 2. ENGINEERS DRAWINGS ARE REQUIRED AND THOSE DRAWINGS MUST TAKE PREFERENCE TO THESE DRAWINGS. 3. ALL BOUNDARY CLEARANCES MUST BE VERIFIED BEFORE COMMENCEMENT OF BUILDING WORKS BY REGISTERED SURVEYOR. 4. BUILDER IS TO STRICTLY COMPLY WITH ALL RELEVANT BUILDING CODE OF AUSTRALIA CONSTRUCTION REQUIREMENTS AND AUSTRALIAN STANDARDS. 5. IN CASE OF ALTERATIONS OR DISCREPANCIES NOTIFY TAYLORED DESIGNS & DRAFTING IMMEDIATELY.	REF: DATE:	AMENDMENT:		PROPOSED: SINGLE STOREY DWELLING		CLIENT: ELA Projects Pty Ltd			
		A	08.07.26	PRELIMINARY PLANS		AT: Lot: 4420, DP: 1313734 No.11 Walla Walla Way, Menangle Park. NSW 2563	PROJECT FILES 	JOB NO: 260120	DATE: 08.07.26	DRAWN: MT
		B	23.07.26	DRP AMENDMENTS				Sheet Size: A2	LGA: Campbelltown City	Sheet: 8 of 9
		C	21.08.26	CDC PLANS						

Landscaped Area Calculation Plan

1:200

Gross Floor Area Calculation Plan

1:100

LOT 4420

DP: 1313734

425.30m²

LEGEND:

AHD	AUSTRALIAN HEIGHT DATUM
AWN	AWNING
BM	BENCH MARK
CL	CENTRE LINE
CONC	CONCRETE
CS	CONCRETE SURFACE
D/H/S	DIAMETER/HEIGHT/SPREAD
D	DOOR
EC	EDGE OF CONCRETE
EG	EAVE & GUTTER
EP	ELECTRICAL BOX
FL	FLOOR LEVEL
GDN	GARDEN
HYD	HYDRANT
IC	INSPECTION COVER
INV	INVERT LEVEL
KO	KERB OUTLET
LH	LAMP HOLE
LIP	LIP OF KERB
NS	NATURAL SURFACE
PAV	PAVERS
PP	POWER POLE
RL	REDUCED LEVEL
S	STEPS
SL	SURFACE LEVEL
SILL	WINDOW SILL
SIP	SEWER INSPECTION POINT
SMH	SEWER MAN HOLE
SV	STOP VALE
TEL	TELSTRA PIT
TK	TOP OF KERB
TOW/TW	TOP OF WALL
TRW	TOP OF RETAINING WALL
VC	VEHICLE CROSSING
WM	WATER METER
WTOP	TOP OF WINDOW

STRRUP LANE

LOT 4419
DP 1313734
VACANT
No.9LOT 4421
DP 1313734
VACANT
No.13PROPOSED
DWELLING

State Environmental Planning
Policy (Exempt and Complying
Development Codes) 2008
Part 3C Greenfield Housing Code Requirements:

LANDSCAPING: (Min 1.5m Wide)
REQUIRED: 15% (63.80m²)
ACHIEVED: 18% (76.88m²)

FRONT YARD LANDSCAPING: (Min 1.5m Wide)
(FRONT YARD = 54.24m²)
REQUIRED: 25% (13.56m²)
ACHIEVED: 41% (23.24m²)

WALLA WALLA WAY

BCA (NCC) & AUSTRALIAN STANDARDS
COMPLIANCE NOTES:

EARTHWORK IS TO COMPLY WITH PART H103 OF NCC 2022 - SITE PREPARATION

TERMITE MANAGEMENT IS TO COMPLY WITH PART H103 OF NCC 2022 - SITE PREPARATION AND AS 3668.1-2014. A DURABLE NOTICE IS TO BE INSTALLED IN ACCORDANCE WITH PART H103 OF NCC 2022. WHERE A CHEMICAL TERMITE MANAGEMENT SYSTEM IS USED, THE CHEMICAL MUST BE INCLUDED ON THE APPROPRIATE AUTHORITY'S PESTICIDES REGISTER

FOOTINGS AND SLABS ARE TO COMPLY WITH AS 2870-2011.

SCALE BAR 1:200

0 2 4 6 8m

SCALE BAR 1:100

0 1,000 2,000 3,000 4,000mm



Phone: 0401 482 401

Email: info@taylorreddesigns.com.au

Copyright. ©

This plan is the property of Taylored Designs & Drafting and may not be used in whole or part

GENERAL NOTES

- LEVELS SHOWN ARE APPROXIMATE AND TO BE CONFIRMED ON SITE BY SURVEYOR.
- ENGINEERS DRAWINGS ARE REQUIRED AND THOSE DRAWINGS MUST TAKE PREFERENCE TO THESE DRAWINGS
- ALL BOUNDARY CLEARANCES MUST BE VERIFIED BEFORE COMMENCEMENT OF BUILDING WORKS BY REGISTERED SURVEYOR.
- BUILDER IS TO STRICTLY COMPLY WITH ALL RELEVANT BUILDING CODE OF AUSTRALIA CONSTRUCTION REQUIREMENTS AND AUSTRALIAN STANDARDS.
- IN CASE OF ALTERATIONS OR DISCREPANCIES NOTIFY TAYLORED DESIGNS & DRAFTING IMMEDIATELY.

REF:	DATE:	AMENDMENT:
A	08.07.26	PRELIMINARY PLANS
B	23.07.26	DRP AMENDMENTS
C	21.08.26	CDC PLANS

PROPOSED: SINGLE STOREY DWELLING

AT: Lot: 4420, DP: 1313734
No.11 Walla Walla Way,
Menangle Park. NSW 2563

PROJECT FILES


CLIENT:
ELA Projects Pty Ltd

JOB NO:	DATE:	DRAWN:
260120	08.07.26	MT
Sheet Size:	LGA:	Sheet:
A2	Campbelltown City	9 of 9



BUSHFIRE BAL-12.5
(In Compliance with AS3959-2018)

FIGURED DIMENSIONS TO BE USED IN
PREFERENCE TO SCALING THIS DRAWING
DO NOT ASSUME - IF IN DOUBT ASK.

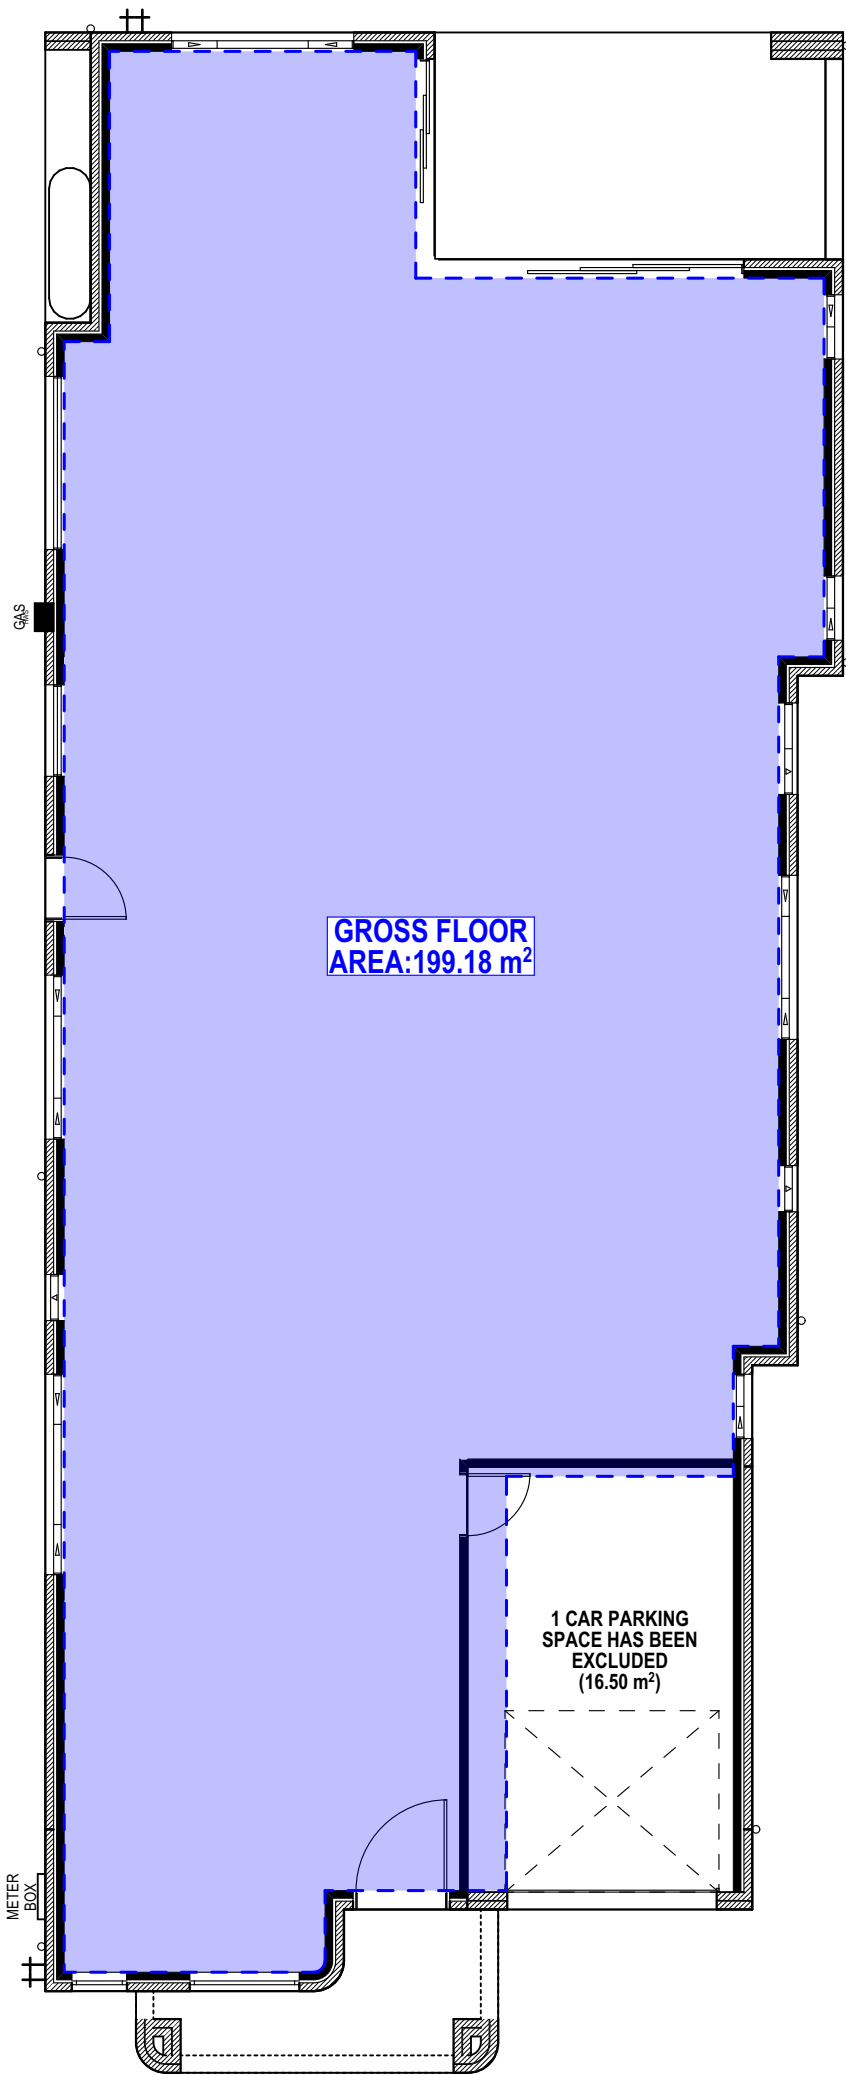

State Environmental Planning
Policy (Exempt and Complying
Development Codes) 2008
Part 3C Greenfield Housing Code Requirements:

GROSS FLOOR AREA:
ALLOWED: 256.32m² (0.25x425.30)+150)
ACHIEVED: 199.18m²