

FOR CONSTRUCTION

LOT 520 IN DP1310900 LOCATED AT 46 GUNYADU STREET AUSTRAL NSW 2179

Proposed Construction of a New Double-Storey Residential Dwelling with Double Garage and Associated Site Works on a Vacant Allotment



BASIX™Certificate

Building Sustainability Index
www.planningportal.nsw.gov.au/development-and-assessment/basix

Single Dwelling

Certificate number: 1851052S

This certificate confirms that the proposed development will meet the NSW government's requirements for sustainability, if it is built in accordance with the commitments set out below. Terms used in this certificate, or in the commitments, have the meaning given by the document entitled "BASIX Definitions" dated 10/09/2020 published by the Department. This document is available at www.planningportal.nsw.gov.au/definitions

Secretary
Date of issue: Friday, 12 June 2026
To be valid, this certificate must be submitted with a development application or lodged with a complying development certificate application within 3 months of the date of issue.



BASIX Department of Planning, Housing and Infrastructure www.basix.nsw.gov.au Version: 4.04 / EUCALYPTUS_03_01_0 Certificate No.: 1851052S Friday, 12 June 2026 page 1/12

Project summary		
Project name	Lot 520 Gunyadu Street Austral	
Street address	GUNYADU STREET AUSTRAL 2179	
Local Government Area	Liverpool City Council	
Plan type and plan number	Deposited Plan dp1310900	
Lot no.	520	
Section no.	-	
Project type	dwelling house (detached)	
No. of bedrooms	5	
Project score		
Water	✔ 40	Target 40
Thermal Performance (Do-it-Yourself Method)	✔ Pass	Target Pass
Energy	✔ 71	Target 70
Materials	✔ -41	Target n/a

Certificate Prepared by	
Name / Company Name:	HOMESVALE PTY LTD.
ABN (if applicable):	76638783150

GENERAL LEGEND

AC	AIR CONDITIONING UNIT
AL	POWDERCOATED ALUMINIUM DOOR/ WINDOW
BAL	BALUSTRADE TYPE
BG	BOX GUTTER
BR1, BR2, etc.	BRICK FACE TYPE
CAP	METAL CAPPING
CD1, CD2, etc.	WALL CLADDING
CONC.	CONCRETE FLOOR
CPT	CARPET
CRT	CONCRETE ROOF TILES
CR1, CR2, etc.	CEMENT RENDER TYPE/ COLOUR
DP/S	DOWN PIPE
DW	DISH WASHER
ED	ENTRY DOOR
F	FRIDGE
FAS	FASCIA
FET	FEATURE TILE
FT, FT1, FT2, etc.	FLOOR TILES
FW	FLOOR WASTE
GD	GARAGE DOOR
GUT	GUTTER
HWU	HOT WATER UNIT
HYB	HYBRID FLOOR
L	LINEN
MR	METAL ROOF
MW	MICROWAVE OVEN
NGL	NATURAL GROUND LEVEL
OBS	OBSURED GLASS
P	PANTRY
R	ROBE
RL	REDUCED LEVEL
RWH	RAIN WATER HEAD
RWT	RAIN WATER TANK
S	STORAGE
TOW	TOP OF WALL
TL	TIMBER LAMINATE
WC	WATER CLOSET
WM	WASHING MACHINE
SD	SMOKE DETECTOR

Sheet List		
Sheet No.	Sheet Name	Revision
CC.01	COVER SHEET	5
CC.02	GENERAL NOTES A	4
CC.02B	GENERAL NOTES B	4
CC.03	LOCATION PLAN AND SITE PLAN	4
CC.04A	SEDIMENT CONTROL PLAN	4
CC.04B	SITE ANALYSIS AND WASTE MANAGEMENT PLAN	4
CC.05	GROUND FLOOR PLAN	4
CC.06	FIRST FLOOR LEVEL	4
CC.07	ROOF PLAN	4

Sheet List		
Sheet No.	Sheet Name	Revision
CC.08	ELEVATION 01	4
CC.09	ELEVATION 02	4
CC.10	SECTIONS	4
CC.11	BUILT UP AREA	4
CC.12	RENTABLE AREA PLAN	4
CC.14	COLOR SCHEDULE	4
CC.15	LANDSCAPE PLAN	4
CC.16	BASIX	4
CC.18	DRIVEWAY PLAN	4
CC.19	WATERPROOFING DETAILS	4

NOTE: ALL IMAGES ARE FOR ILLUSTRATION ONLY AND ARE SUBJECT TO VARIATION AND TO AVAILABILITY OF MATERIALS.

REV	DATE	DESCRIPTION	BY
5	26-08-2026	CC ISSUE	
4	7-07-2026	Site Address updated	
3	23-06-2026	DA ISSUE	
1	02-04-2026	Bank Set	



THIS DRAWING IS THE EXCLUSIVE PROPERTY OF THE DEVELOPER & THE REPRODUCTION OF ANY PART WITHOUT THE PRIOR WRITTEN CONSENT OF THE DEVELOPER IS A VIOLATION OF APPLICABLE LAWS. IN NO EVENT SHALL THE DEVELOPER BE HELD LIABLE FOR SPECIAL COLLATERAL, INCIDENTAL OR CONSEQUENTIAL LIABILITY IN CONNECTION WITH THE USE OF THIS DIGITAL DATA ONCE RELEASED FROM THE DEVELOPER'S OFFICE. THIS DRAWING IS TO BE READ & UNDERSTOOD IN CONJUNCTION WITH THE STRUCTURAL, MECHANICAL, ELECTRICAL & / OR ANY OTHER CONSULTANT'S DOCUMENTATION AS MAY BE APPLICABLE TO THE PROJECT PRIOR TO THE START OF ANY WORKS AND FOR ITS DURATION.

PROJECT:
46 Gunyadu Street

Lot 520 in Dp 1310900 at 46
Gunyadu Street Austral NSW 2179

DRAWING TITLE:
COVER SHEET

NORTH:

LOT NO:
520

DRAWN BY:
AS

DRAFTED BY:
SL

DATE:
7-09-2026

CHECKED BY:
RH

CLIENT NAME:
Anushka Gartaula Siwakoti

SCALE:
1 : 100

DRAWING No:
CC.01

REV:
5

ISSUED BY:

BUILDING SPECIFICATIONS

**National Construction Code – Volume 2,
Amendment 1 – Building Code of Australia 2022
& Housing Provisions Standard 2022**

SITE PREPARATION

- PART 3.1 OF THE NCC VOLUME 2, AMENDMENT 1 - BUILDING CODE OF AUSTRALIA 2022 & HOUSING PROVISIONS STANDARD 2022

EARTHWORKS

- TO BE CARRIED OUT IN ACCORDANCE WITH THE REQUIREMENTS OF THE ENVIRONMENTAL PLANNING & ASSESSMENT ACT 1979 AND DEVELOPMENT CONSENT CONDITIONS
- PART 3.2 OF THE NCC VOLUME 2, AMENDMENT 1 - BUILDING CODE OF AUSTRALIA 2022 & HOUSING PROVISIONS STANDARD 2022.
- AS 4678:2002 - EARTH-RETAINING STRUCTURES

DRAINAGE

- PART 3.3 OF THE NCC VOLUME 2, AMENDMENT 1 - BUILDING CODE OF AUSTRALIA 2022 & HOUSING PROVISIONS STANDARD 2022.
- AS/NZS 3500.1:2021 - PLUMBING & DRAINAGE - WATER SERVICES
- AS/NZS 3500.2:2021 - PLUMBING & DRAINAGE - SANITARY PLUMBING & DRAINAGE
- AS/NZS 3500.3:2021 - PLUMBING & DRAINAGE - STORMWATER DRAINAGE
- AS/NZS 3500.4:2021 - PLUMBING & DRAINAGE - HEATED WATER SERVICES

STRUCTURAL WORK

- Part 2.2 OF THE NCC VOLUME 2, AMENDMENT 1 - BUILDING CODE OF AUSTRALIA 2022 & HOUSING PROVISIONS STANDARD 2022.
- AS 4100:2020 - STEEL STRUCTURES CODES
- AS/NZS 1170.0:2002 - GENERAL PRINCIPLES
- AS/NZS 1170.1:2002 - PARTS 1 PERMANENT, IMPOSED AND OTHER ACTIONS
- AS/NZS 1170.2:2021 - PART 2 WIND ACTIONS
- AS 3700:2018 - SAA MASONRY CODE
- AS 1684.3:2021 - RESIDENTIAL TIMBER FRAMED CONSTRUCTION

FOOTINGS & SLABS

- PART 4 OF THE NCC VOLUME 2, AMENDMENT 1 - BUILDING CODE OF AUSTRALIA 2022 & HOUSING PROVISIONS STANDARD 2022.
- AS 2159:2009 - PILING - DESIGN & INSTALLATION
- AS 2870:2011 - RESIDENTIAL SLABS & FOOTINGS
- AS 3600:2018 - CONCRETE STRUCTURES

MASONRY

- PART 5 OF THE NCC VOLUME 2, AMENDMENT 1 - BUILDING CODE OF AUSTRALIA 2022 & HOUSING PROVISIONS STANDARD 2022.
- AS 3700:2018 - MASONRY STRUCTURES
- PART 6 OF THE NCC VOLUME 2, AMENDMENT 1 - BUILDING CODE OF AUSTRALIA 2022 & HOUSING PROVISIONS STANDARD 2022.
- AS 1684.2:2021 - RESIDENTIAL TIMBER-FRAMED CONSTRUCTION - NON- CYCLONIC AREAS
- AS 1720.1:2010 - TIMBER STRUCTURES - DESIGN METHODS
- AS 4100:2020 - STEEL STRUCTURES
- AS 3660.1:2014 - TERMITE MANAGEMENT SYSTEM

ROOF & WALL CLADDING

- PART 7 OF THE NCC VOLUME 2, AMENDMENT 1 - BUILDING CODE OF AUSTRALIA 2022 & HOUSING PROVISIONS STANDARD 2022.
- AS 1273:1991 - UNPLASTICIZED PVC (UPVC) DOWNPIPES & FITTINGS FOR RAINWATER
- AS 1562.1:2018 - DESIGN & INSTALLATION OF SHEET ROOF & WALL CLADDING - METAL
- AS/NZS 1562.3:2006 - DESIGN & INSTALLATION OF SHEET ROOF & WALL CLADDING - PLASTIC
- AS 2049:2002 - ROOF TILES
- AS 2050:2018 - INSTALLATION OF ROOF TILES
- AS 4285:2019 - ROOFLIGHTS

GLAZING

- PART 8 OF THE NCC VOLUME 2, AMENDMENT 1 - BUILDING CODE OF AUSTRALIA 2022 & HOUSING PROVISIONS STANDARD 2022.
- AS 1288:2021 - GLASS IN BUILDINGS - SELECTION & INSTALLATION
- AS 2047:2014 - WINDOWS & EXTERNAL GLAZED DOORS IN BUILDINGS
- AS/NZS 2208:1996 - SAFETY GLAZING MATERIALS IN BUILDINGS

FIRE SAFETY

- PART 9 OF THE NCC VOLUME 2, AMENDMENT 1 - BUILDING CODE OF AUSTRALIA 2022 & HOUSING PROVISIONS STANDARD 2022.
- AS 3786:2014 - SMOKE ALARMS USING SCATTERED LIGHT, TRANSMITTED LIGHT OR IONIZATION

HEALTH & AMENITY

- PART 10 OF THE NCC VOLUME 2, AMENDMENT 1 - BUILDING CODE OF AUSTRALIA 2022 & HOUSING PROVISIONS STANDARD 2022.
- AS/NZS ISO 717.1:2004 - ACOUSTICS - RATING OF SOUND INSULATION IN BUILDINGS & OF BUILDING ELEMENTS - AIRBORNE SOUND INSULATION
- AS ISO 717.2:2004 - ACOUSTICS - RATING OF SOUND INSULATION IN BUILDINGS & OF BUILDING ELEMENTS - IMPACT SOUND INSULATION
- AS 1668.2:2012 - THE USE OF VENTILATION & AIR CONDITIONING IN BUILDINGS - MECHANICAL VENTILATION IN BUILDINGS
- AS 1668.4:2012 - THE USE OF VENTILATION & AIR CONDITIONING IN BUILDINGS - NATURAL VENTILATION OF BUILDINGS
- AS/NZS 1680.0:2009 - INTERIOR LIGHTING - SAFE MOVEMENT
- AS 3740:2021 - WATERPROOFING OF DOMESTIC WET AREAS
- AS 3000:2018 - ELECTRICAL INSTALLATION
- BCA Part 10.8.1, AS4200.1 & AS4200.2 - PLIABLE BUILDING MEMBRANE INSTALLED.

WATERPROOFING

- PART 10.2 OF THE NCC VOLUME 2, AMENDMENT 1 - BUILDING CODE OF AUSTRALIA 2022 & HOUSING PROVISIONS STANDARD 2022
- AS 3740:2021 - WATERPROOFING TO WET AREA
- AS 4654:2012 - EXTERNAL WET AREAS

SAFE MOVEMENT & ACCESS

- PART 11 OF THE NCC VOLUME 2, AMENDMENT 1 - BUILDING CODE OF AUSTRALIA 2022 & HOUSING PROVISIONS STANDARD 2022.
- AS 1428.1:2009 - DESIGN FOR ACCESS & MOBILITY - GENERAL REQUIREMENTS FOR ACCESS - NEW BUILDING WORK
- AS 1657:2018 - FIXED PLATFORMS, WALKWAYS, STAIRWAYS & LADDERS - DESIGN, CONSTRUCTION & INSTALLATION

HANDRAILS & BALUSTRADE

- PART 11.3.3 OF THE NCC VOLUME 2, AMENDMENT 1 - BUILDING CODE OF AUSTRALIA 2022 & HOUSING PROVISIONS STANDARD 2022.
- PART 11.3.4 OF THE NCC VOLUME 2, AMENDMENT 1 - BUILDING CODE OF AUSTRALIA 2022 & HOUSING PROVISIONS STANDARD 2022.
- PART 11.3.5 OF THE NCC VOLUME 2, AMENDMENT 1 - BUILDING CODE OF AUSTRALIA 2022 & HOUSING PROVISIONS STANDARD 2022.
- AS 1170.1:2002 - BALUSTRADE INSTALLATION

PROTECTION OF OPENABLE WINDOW


PART 11.3.7 AND 11.3.8 OF THE NCC VOLUME 2, AMENDMENT 1 - BUILDING CODE OF AUSTRALIA 2022 & HOUSING PROVISIONS STANDARD 2022.

ENERGY EFFICIENCY

- PART 13 OF THE NCC VOLUME 2, AMENDMENT 1 - BUILDING CODE OF AUSTRALIA 2022 & HOUSING PROVISIONS STANDARD 2022 & BASIX CERTIFICATE.

MECHANICAL VENTILATION

- EXHAUST FROM A BATHROOM, SANITARY COMPARTMENT TO DISCHARGE DIRECTLY TO OUTDOOR AIR WITH MINIMUM FLOW RATE OF 25L/S & MAKE-UP AIR VIA OPENINGS TO AN ADJACENT ROOM WITH A FREE AREA OF 14,000 MM². THIS EXHAUST SYSTEM MUST BE INTERLOCKED WITH LIGHT SWITCH AND INCLUDE RUN-ON TIMER SO THAT THE EXHAUST SYSTEM CONTINUES TO OPERATE FOR 10 MINUTES AFTER THE LIGHT SWITCH IS OFF.
- ANY INSTALLED - KITCHEN RANGEHOOD EXHAUST TO DISCHARGE DIRECTLY OR VIA DUCT TO OUTDOOR AIR WITH MINIMUM FLOW RATE OF 40L/S & MAKE-UP AIR VIA OPENINGS TO AN ADJACENT ROOM WITH A FREE AREA OF 14,000 MM².
- LAUNDRY EXHAUST TO DISCHARGE DIRECTLY OR VIA DUCT TO OUTDOOR AIR WITH MINIMUM FLOW RATE OF 40L/S & MAKE-UP AIR VIA OPENINGS TO AN ADJACENT ROOM WITH A FREE AREA OF 14,000 MM².

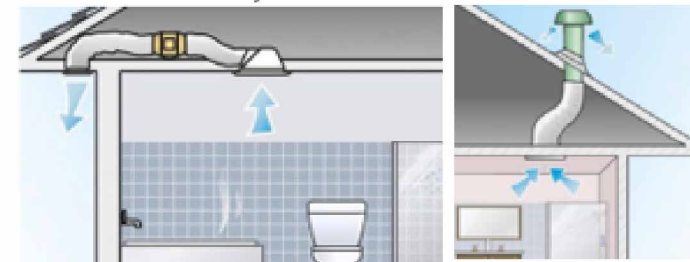

REV	DATE	DESCRIPTION	BY
4	7-07-2026	Site Address updated	
3	23-06-2026	DA ISSUE	



THIS DRAWING IS THE EXCLUSIVE PROPERTY OF THE DEVELOPER & THE REPRODUCTION OF ANY PART WITHOUT THE PRIOR WRITTEN CONSENT OF THE DEVELOPER IS A VIOLATION OF APPLICABLE LAWS. IN NO EVENT SHALL THE DEVELOPER BE HELD LIABLE FOR SPECIAL, COLLATERAL, INCIDENTAL OR CONSEQUENTIAL LIABILITY IN CONNECTION WITH THE USE OF THIS DIGITAL DATA ONCE RELEASED FROM THE DEVELOPER'S OFFICE. THIS DRAWING IS TO BE READ & UNDERSTOOD IN CONJUNCTION WITH THE STRUCTURAL, MECHANICAL, ELECTRICAL & / OR ANY OTHER CONSULTANT'S DOCUMENTATION AS MAY BE APPLICABLE TO THE PROJECT PRIOR TO THE START OF ANY WORKS AND FOR ITS DURATION.

PROJECT:
46 Gunyadu Street

Lot 520 in Dp 1310900 at 46 Gunyadu Street Austral NSW 2179


DRAWING TITLE:
GENERAL NOTES A

NORTH:

CC ISSUE					
LOT NO:	DATE:	SCALE:	DRAWING No:	REV:	
520	7-09-2026	1 : 2	CC.02	4	
DRAWN BY:	CHECKED BY:			ISSUED BY:	
AS	RH				
DRAFTED BY:	CLIENT NAME:				
SL	Anushka Gartaula Siwakoti				


TERMITE SHEET

- TERMITE SHEET EXTENDS THROUGH THE ENTIRE MASONRY LEAF AND IS VISIBLE AT THE FINISHED FACE OF THE WALL.

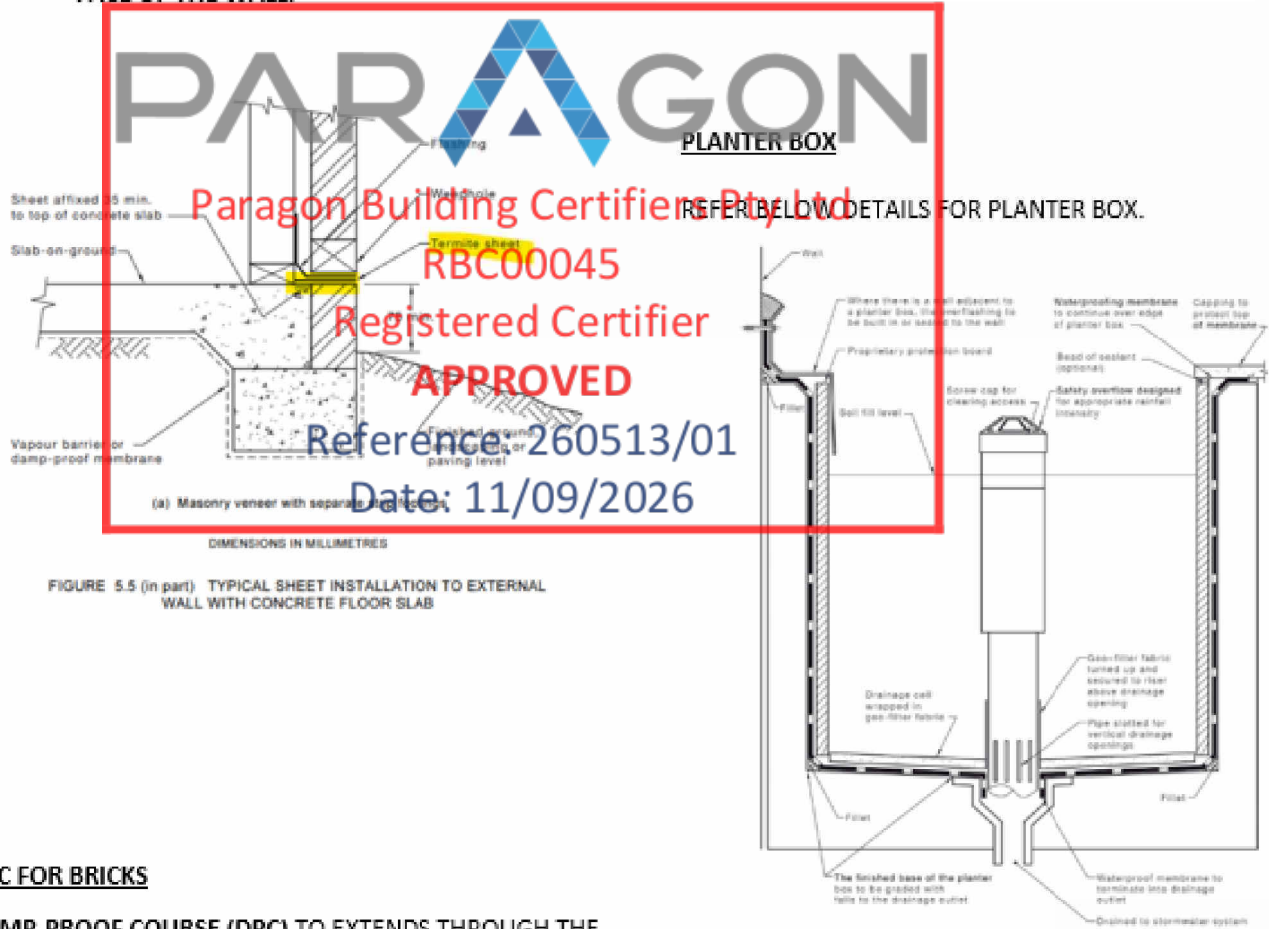


DPC FOR BRICKS

DAMP-PROOF COURSE (DPC) TO EXTENDS THROUGH THE ENTIRE MASONRY LEAF AND NEED TO BE VISIBLE AT THE FINISHED FACE OF THE WALL FROM OUTSIDE

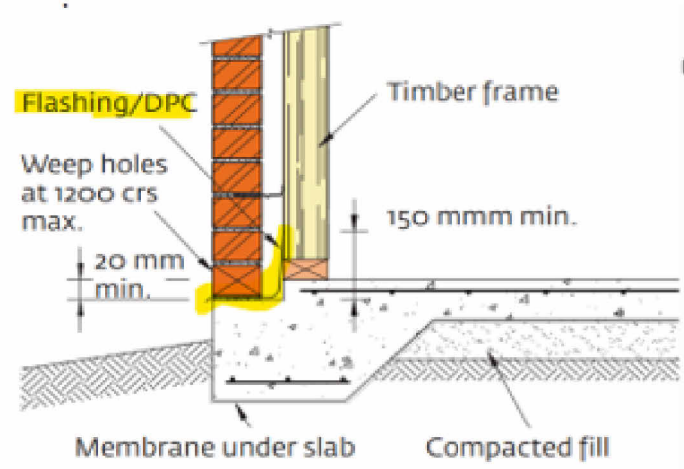

OVERFLOW TO BALCONY:

- SURFACE DRAIN & OVERFLOW TO BALCONY

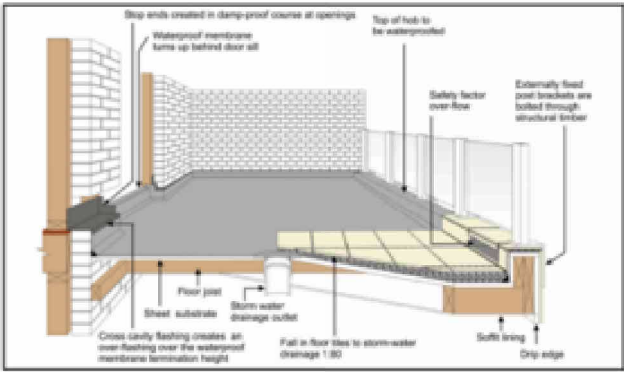

				CC ISSUE								
				 THIS DRAWING IS THE EXCLUSIVE PROPERTY OF THE DEVELOPER & THE REPRODUCTION OF ANY PART WITHOUT THE PRIOR WRITTEN CONSENT OF THE DEVELOPER IS A VIOLATION OF APPLICABLE LAWS. IN NO EVENT SHALL THE DEVELOPER BE HELD LIABLE FOR SPECIAL COLLATERAL, INCIDENTAL OR CONSEQUENTIAL LIABILITY IN CONNECTION WITH THE USE OF THIS DIGITAL DATA ONCE RELEASED FROM THE DEVELOPER'S OFFICE. THIS DRAWING IS TO BE READ & UNDERSTOOD IN CONJUNCTION WITH THE STRUCTURAL, MECHANICAL, ELECTRICAL & / OR ANY OTHER CONSULTANT'S DOCUMENTATION AS MAY BE APPLICABLE TO THE PROJECT PRIOR TO THE START OF ANY WORKS AND FOR ITS DURATION.	PROJECT: 46 Gunyadu Street	DRAWING TITLE: GENERAL NOTES B	NORTH:	LOT NO:	DATE:	SCALE:	DRAWING No:	REV:
520	7-09-2026	1 : 2	CC.02B					4				
								DRAWN BY:	CHECKED BY:	ISSUED BY:		
		AS	RH									
				Lot 520 in Dp 1310900 at 46 Gunyadu Street Austral NSW 2179				DRAFTED BY:	CLIENT NAME:			
		SL	Anushka Gartaula Siwakoti									
REV	DATE	DESCRIPTION	BY									
4	7-07-2026	Site Address updated										
3	23-06-2026	DA ISSUE										



THIS DRAWING IS THE EXCLUSIVE PROPERTY OF THE DEVELOPER & THE REPRODUCTION OF ANY PART WITHOUT THE PRIOR WRITTEN CONSENT OF THE DEVELOPER IS A VIOLATION OF APPLICABLE LAWS. IN NO EVENT SHALL THE DEVELOPER BE HELD LIABLE FOR SPECIAL COLLATERAL, INCIDENTAL OR CONSEQUENTIAL LIABILITY IN CONNECTION WITH THE USE OF THIS DIGITAL DATA ONCE RELEASED FROM THE DEVELOPER'S OFFICE. THIS DRAWING IS TO BE READ & UNDERSTOOD IN CONJUNCTION WITH THE STRUCTURAL, MECHANICAL, ELECTRICAL & / OR ANY OTHER CONSULTANT'S DOCUMENTATION AS MAY BE APPLICABLE TO THE PROJECT PRIOR TO THE START OF ANY WORKS AND FOR ITS DURATION.

GUNYADU STREET

GUNYADU STREET

CC - SITE PLAN

1 : 200

BULUNGA STREET

SITE CUT & FILL

2 : 200

BULUNGA STREET

COMPLIANCE TABLE

Liverpool Growth Centres Precincts Development Control Plan

DESCRIPTION		COMPLIANCE		COMMENT
ELEMENT	CODE CONTROL	REQUIREMNT	PROPOSED	
LAND ZONE	R2 - Low Density Residential			
LOT NO	LOT 520			
LOT AREA	361.1 m ²			
LOT WIDTH	14.5m	≥ 9m and ≤15m	11m (MAX.)	
HEIGHT	MAX. Height	9m	8.1m (MAX.)	
FRONT SETBACK	4.5m to building facade line; 3.0m to articulation zone;	4.5 m	4.8m	YES
REAR SET BACK (MIN.)	GROUND FLOOR	4m	7m	YES
	FIRST FLOOR	6m	12.7m	
SIDE SET BACK (MIN.) Corner Lot	GROUND FLOOR	0.9/2.0m	0.95/2.36m	YES
	FIRST FLOOR	0.9/2.0m	0.95/2.36m	
SITE COVERAGE	GROUND FLOOR	60%	104 m ² (28.8%)	YES
	FIRST FLOOR	40%	86 m ² (23.8%)	
LANDSCAPE AREA	25 % of TOTAL LAND AREA	90.275 m ²	162.3 m ²	YES
Principal Private Open space (PPOS)	>10m Lot width	24m ²	24 m ²	YES
Garages and car parking	Front or rear accessed single, tandem or double garages permitted Triple garages are not permitted.		SIDE DOUBLE GARAGE	

CUT UPTO 200-400	
CUT UPTO 200	
FILL UPTO 200	
FILL UPTO 200-400	
FILL UPTO 400-600	



THIS DRAWING IS THE EXCLUSIVE PROPERTY OF THE DEVELOPER & THE REPRODUCTION OF ANY PART WITHOUT THE PRIOR WRITTEN CONSENT OF THE DEVELOPER IS A VIOLATION OF APPLICABLE LAWS. IN NO EVENT SHALL THE DEVELOPER BE HELD LIABLE FOR SPECIAL COLLATERAL, INCIDENTAL OR CONSEQUENTIAL LIABILITY IN CONNECTION WITH THE USE OF THIS DIGITAL DATA ONCE RELEASED FROM THE DEVELOPER'S OFFICE. THIS DRAWING IS TO BE READ & UNDERSTOOD IN CONJUNCTION WITH THE STRUCTURAL, MECHANICAL, ELECTRICAL & / OR ANY OTHER CONSULTANT'S DOCUMENTATION AS MAY BE APPLICABLE TO THE PROJECT PRIOR TO THE START OF ANY WORKS AND FOR ITS DURATION.

PROJECT:
46 Gunyadu Street

Lot 520 in Dp 1310900 at 46
Gunyadu Street Austral NSW 2179

DRAWING TITLE:
LOCATION PLAN
AND SITE PLAN







LOT NO: 520	DATE: 7-09-2026	SCALE: As indicated	DRAWING No: CC.03	REV: 4
DRAWN BY: AS	CHECKED BY: RH		ISSUED BY:	
DRAFTED BY: SL	CLIENT NAME: Anushka Gartaula Siwakoti			

REV	DATE	DESCRIPTION	BY
4	7-07-2026	Site Address updated	
3	23-06-2026	DA ISSUE	



SEDIMENT CONTROL PLAN

1
1 : 200

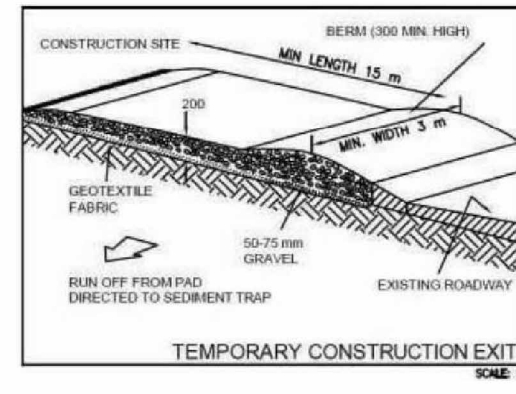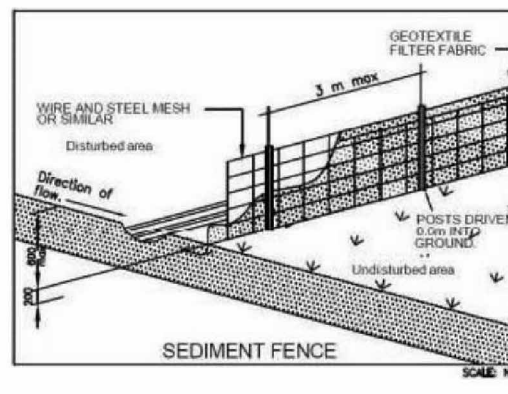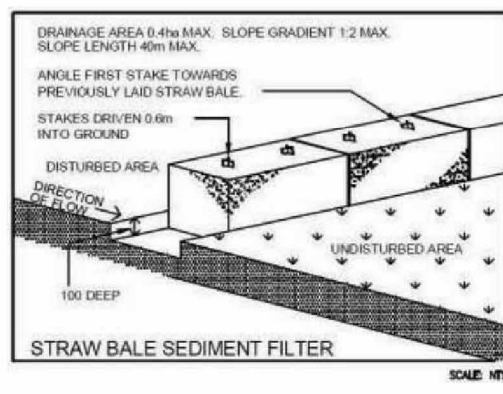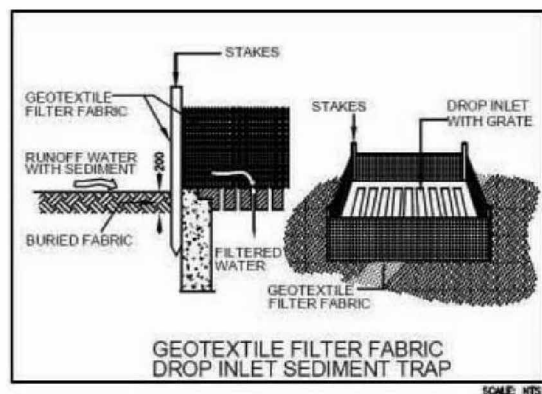

SEDIMENT AND EROSION NOTES:

- THIS PLAN TO BE READ IN CONJUNCTION WITH SEDIMENT AND EROSION CONTROL DETAILS AS ATTACHED.
- THE CONTRACTOR SHALL IMPLEMENT ALL SOIL EROSION AND SEDIMENT CONTROL MEASURES AS NECESSARY AND TO THE SATISFACTION OF COUNCIL PRIOR TO THE COMMENCEMENT AND DURING CONSTRUCTION. NO DISTURBANCE TO THE SITE SHALL BE PERMITTED OTHER THAN IN THE IMMEDIATE AREA OF THE WORK AND NO MATERIAL SHALL BE REMOVED FROM THE SITE WITHOUT COUNCIL'S APPROVAL. ALL SEDIMENT AND EROSION CONTROL DEVICES TO BE INSTALLED AND MAINTAINED IN ACCORDANCE WITH STANDARDS OUTLINED IN NSW DEPARTMENT OF HOUSING "MANAGING URBAN STORMWATER-SOILS AND CONSTRUCTIONS".
- TOPSOIL SHALL BE STRIPPED AND STOCKPILED OUTSIDE HAZARD AREAS SUCH AS DRAINAGE LINES. THIS TOP SOIL IS TO BE RESPIRED LATER ON AREAS TO BE REVEGETATED AND STABILISED ONLY. (I.E ALL FOOTPATHS, BATTERS, SITE REGARDING AREAS, BASINS AND CATCH DRAINS). TOPSOIL SHALL NOT BE RESPIRED ON ANY OTHER AREAS UNLESS SPECIALLY INSTRUCTED BY THE SUPERIDENT. IF THEY ARE TO REMAIN FOR LONGER THAN ONE MONTH STOCKPILES SHALL BE PROTECTED FROM EROSION BY COVERING THEM WITH A MULCH AND HYDROSEEDING AND, IF NECESSARY, BY LOCATING BANKS OR DRAINS DOWNSTREAM OF A STOCKPILE TO RETARD SILT LADEN RUNOFF.
- THE CONTRACTOR SHALL REGULARLY MAINTAIN ALL SEDIMENT AND EROSION CONTROL DEVICES AND REMOVE ACCUMULATED SILT FROM SUCH DEVICES SUCH THAT MORE THAN 60% OF THEIR CAPACITY LOST. ALL THE SILTS TO BE PLACED OUTSIDE THE LIMIT OF WORKS. THE PERIOD FOR MAINTAINING THESE DEVICES SHALL BE AT LEAST UNTIL ALL DISTURBED AREAS ARE REVEGETATED AND FURTHER AS MAY BE DIRECTED BY THE SUPERINTENDENT OR COUNCIL.
- LAY TURF STRIP (MIN 300 mm WIDE) ON 100 mm TOPSOIL WITH 1.0 m LONG RETURNS EVERY 6.0m BEHIND ALL KERB AT THE TOP OF ALL BATTERS AND AROUND STRUCTURES IMMEDIATELY AFTER BACKFILLING OR FORMATION.
- THE CONTRACTOR SHALL GRASS SEED ALL DISTURBED AREAS WITH AN APPROVED MIX AS SSON AS PRACTICABLE AFTER COMPLETION OF EARTHWORKS AND REGRADING.
- VEHICULAR TRAFFIC SHALL BE CONTROLLED DURING CONSTRUCTION CONFINING ACCESS WHERE POSSIBLE TO NOMINATED STABILISED ACCESS POINTS.
- WHEN ANY DEVICES ARE TO BE HANDED OVER TO COUNCIL, THEY SHALL BE IN CLEAN AND STABLE CONDITION.
- THE CONTRACTOR SHALL IMPLEMENT DUST CONTROL BY REGULAR WETTING DOWN (BUT NOT SATURATING) DISTURBED AREA.
- PROVIDE AND MAINTAIN SILT TRAPS AROUND ALL SURFACE INLET PITS UNTIL CATCHMENT IS REVEGETATED OR PAVED.
- REVEGETATE ALL TRENCHES IMMEDIATELY UPON COMPLETION OF BACKFILLING.
- ALL DRAINAGE PIPE INLETS TO BE CAPPED UNTIL:
 - A) DOWNPIPES CONNECTED
 - B) PITS CONSTRUCTED & PROTECTED WITH SILT BARRIER

SD 6-9 GEOTEXTILE INLET FILTER

- 1) FABRICATE A SEDIMENT BARRIER MADE FROM GEOTEXILE. REFER SD6-7 FOR DETAILS.
- 2) SUPPORT GEOTEXILE WITH MESH TIED TO POSTS AT 1 m Ctrs.
- 3) DO NOT COVER INLET WITH GEOTEXILE.

SITE WORKS NOTES

1. ORIGIN OF LEVELS PROVIDED BY SURVEYOR
2. THE BUILDER SHALL VERIFY ALL DIMENSIONS AND EXISTING LEVELS ON SITE PRIOR TO THE COMMENCEMENT OF WORK AND ANY DISCREPANCIES SHALL BE REPORTED TO THE SURVEYOR / ENGINEER.
3. TOPSOIL SHALL BE STRIPPED FROM THE CONSTRUCTION AREA AND STOCKPILED ON SITE, TO BE LATER SPREAD OR DISPOSED OFF SITE AS DIRECTED BY SUPERVISOR / ENGINEER.
4. ALL TRENCH BACKFILL MATERIAL SHALL BE COMPACTED TO THE SAME DENSITY AS THE ADJACENT MATERIAL.
5. ALL SERVICE TRENCHES UNDER VEHICULAR PAVEMENTS SHALL BE BACKFILLED WITH SAND OR APPROVED GRANULAR MATERIALS. TO THE UNDERSIDE OF THE PAVEMENT, AND COMPACTED TO 98% STANDARD MAXIMUM DRY DENSITY, IN ACCORDANCE WITH AS 1289E1.1.

SD 5-7 STABILISED SITE ACCESS

- 1) STRIP TOPSOIL AND LEVEL SITE.
- 2) COMPACT SUBGRADE.
- 3) COVER AREA WITH GEOTEXILE.
- 4) CONSTRUCT 200 mm THICK PAD OVER GEOTEXILE USING ROADBASE OR 30 mm AGGREGATE. Min 15 m LONG OR TO BUILDING ALIGNMENT. Min 3 m WIDE.
- 5) CONSTRUCT HUMPS IMMEDIATELY WITHIN BOUNDARY TO DIVERT WATER TO A SEDIMENT FENCE OR OTHER SEDIMENT TRAP.

CC ISSUE

REV	DATE	DESCRIPTION	BY
4	7-07-2026	Site Address updated	
3	23-06-2026	DA ISSUE	

RUBY HOMES

THIS DRAWING IS THE EXCLUSIVE PROPERTY OF THE DEVELOPER AND THE REPRODUCTION OF ANY PART WITHOUT THE PRIOR WRITTEN CONSENT OF THE DEVELOPER IS A VIOLATION OF APPLICABLE LAWS. IN NO EVENT SHALL THE DEVELOPER BE HELD LIABLE FOR SPECIAL COLLATERAL, INCIDENTAL OR CONSEQUENTIAL LIABILITY IN CONNECTION WITH THE USE OF THIS DIGITAL DATA ONCE RELEASED FROM THE DEVELOPER'S OFFICE. THIS DRAWING IS TO BE READ & UNDERSTOOD IN CONJUNCTION WITH THE STRUCTURAL, MECHANICAL, ELECTRICAL & / OR ANY OTHER CONSULTANT'S DOCUMENTATION AS MAY BE APPLICABLE TO THE PROJECT PRIOR TO THE START OF ANY WORKS AND FOR ITS DURATION.

PROJECT:
46 Gunyadu Street


Lot 520 in Dp 1310900 at 46
Gunyadu Street Austral NSW 2179

DRAWING TITLE:
SEDIMENT CONTROL PLAN



LOT NO:	DATE:	SCALE:	DRAWING No:	REV:
520	7-09-2026	As indicated	CC.04A	4
DRAWN BY:	CHECKED BY:			ISSUED BY:
AS	RH			
DRAFTED BY:	CLIENT NAME:			
SL	Anushka Gartaula Siwakoti			

IMPORTANT NOTES:
ALL DIMENSIONS AND NOTES ON ALL PLANS MUST BE CHECKED AND VERIFIED BY BUILDERS AND OWNER PRIOR TO COMMENCEMENT OF ANY BUILDING WORKS. TO CLARIFY AND CONFIRM WITH CONSTRUCTION COMPANY FOR DISCREPANCIES ON ALL DOCUMENTS AND PLANS PROVIDED FOR CONSTRUCTION. ANY WORK INDICATED ON THE PLAN BUT NOT IN THE SPECIFICATION BUT WHICH IS NECESSARY AS PART OF THE CONTRACT, VARIATION TO PLANS, SPECIFICATIONS MAY NOT BE MADE WITHOUT THE WRITTEN CONSENT OF OWNER. IT IS THE RESPONSIBILITY OF THE BUILDER/END USER TO VERIFY PLANS AND SPECIFICATIONS AS TO THEIR ACCURACY AND COMPLY CURRENT BCA AND AUSTRALIAN STANDARDS. WINDOWS TO COMPLY WITH 3.9.3.5 OF THE BCA.

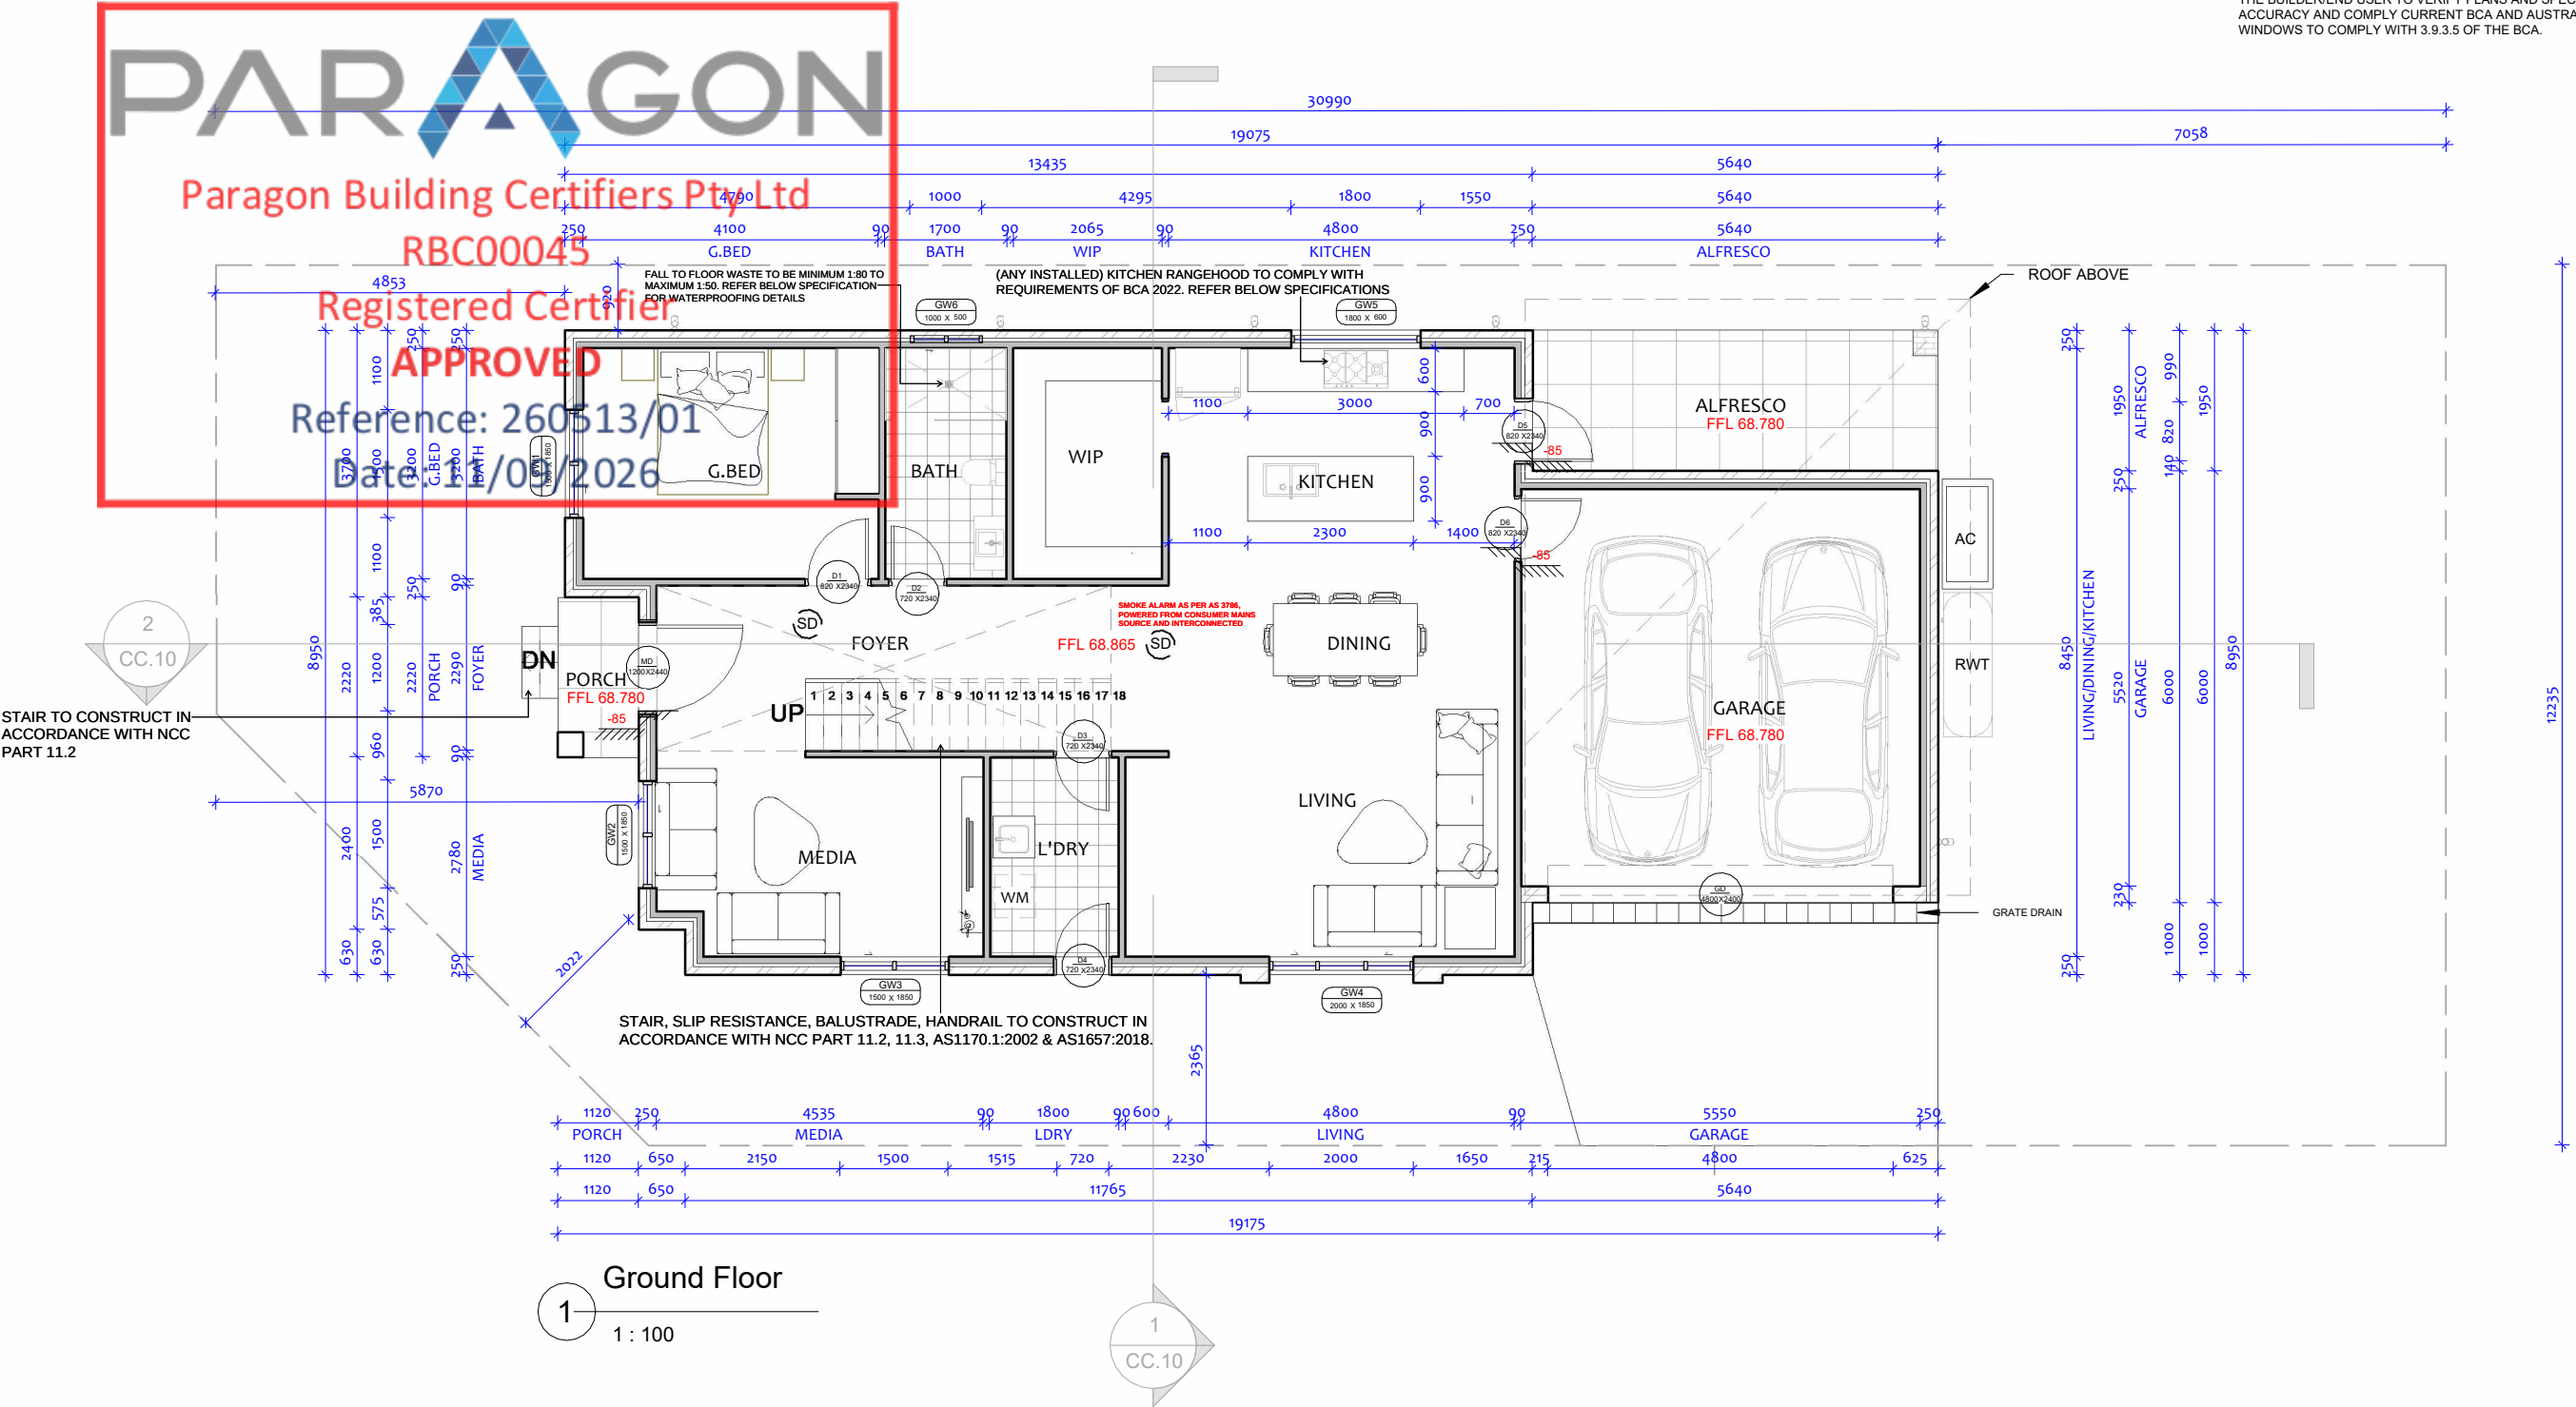

Riser and going dimensions (mm)

Stair type	Riser (R)		Going (G)		Slope relationship (2R+G)	
	Max	Min	Max	Min	Max	Min
Stairs	190	115	355	240	700	550

NOTE: PLEASE REFER TO TENDER FOR ALL INCLUSIONS.

REV	DATE	DESCRIPTION	BY
4	7-07-2026	Site Address updated	
3	23-06-2026	DA ISSUE	
1	02-04-2026	Bank Set	

THIS DRAWING IS THE EXCLUSIVE PROPERTY OF THE DEVELOPER & THE REPRODUCTION OF ANY PART WITHOUT THE PRIOR WRITTEN CONSENT OF THE DEVELOPER IS A VIOLATION OF APPLICABLE LAWS. IN NO EVENT SHALL THE DEVELOPER BE HELD LIABLE FOR SPECIAL COLLATERAL, INCIDENTAL OR CONSEQUENTIAL LIABILITY IN CONNECTION WITH THE USE OF THIS DIGITAL DATA ONCE RELEASED FROM THE DEVELOPER'S OFFICE. THIS DRAWING IS TO BE READ & UNDERSTOOD IN CONJUNCTION WITH THE STRUCTURAL, MECHANICAL, ELECTRICAL & / OR ANY OTHER CONSULTANT'S DOCUMENTATION AS MAY BE APPLICABLE TO THE PROJECT PRIOR TO THE START OF ANY WORKS AND FOR ITS DURATION.

PROJECT:
46 Gunyadu Street



Lot 520 in Dp 1310900 at 46 Gunyadu Street Austral NSW 2179

DRAWING TITLE:
GROUND FLOOR PLAN

NORTH:

LOT NO: 520	DATE: 7-09-2026	SCALE: 1 : 100	DRAWING No: CC.05	REV: 4
DRAWN BY: AS	CHECKED BY: RH			ISSUED BY:
DRAFTED BY: SL	CLIENT NAME: Anushka Gartaula Siwakoti			

IMPORTANT NOTES:
ALL DIMENSIONS AND NOTES ON ALL PLANS MUST BE CHECKED AND VERIFIED BY BUILDERS AND OWNER PRIOR TO COMMENCEMENT OF ANY BUILDING WORKS. TO CLARIFY AND CONFIRM WITH CONSTRUCTION COMPANY FOR DISCREPANCIES ON ALL DOCUMENTS AND PLANS PROVIDED FOR CONSTRUCTION. ANY WORK INDICATED ON THE PLAN BUT NOT IN THE SPECIFICATION BUT WHICH IS NECESSARY AS PART OF THE CONTRACT, VARIATION TO PLANS, SPECIFICATIONS MAY NOT BE MADE WITHOUT THE WRITTEN CONSENT OF OWNER. IT IS THE RESPONSIBILITY OF THE BUILDER/END USER TO VERIFY PLANS AND SPECIFICATIONS AS TO THEIR ACCURACY AND COMPLY CURRENT BCA AND AUSTRALIAN STANDARDS. WINDOWS TO COMPLY WITH 3.9.3.5 OF THE BCA.

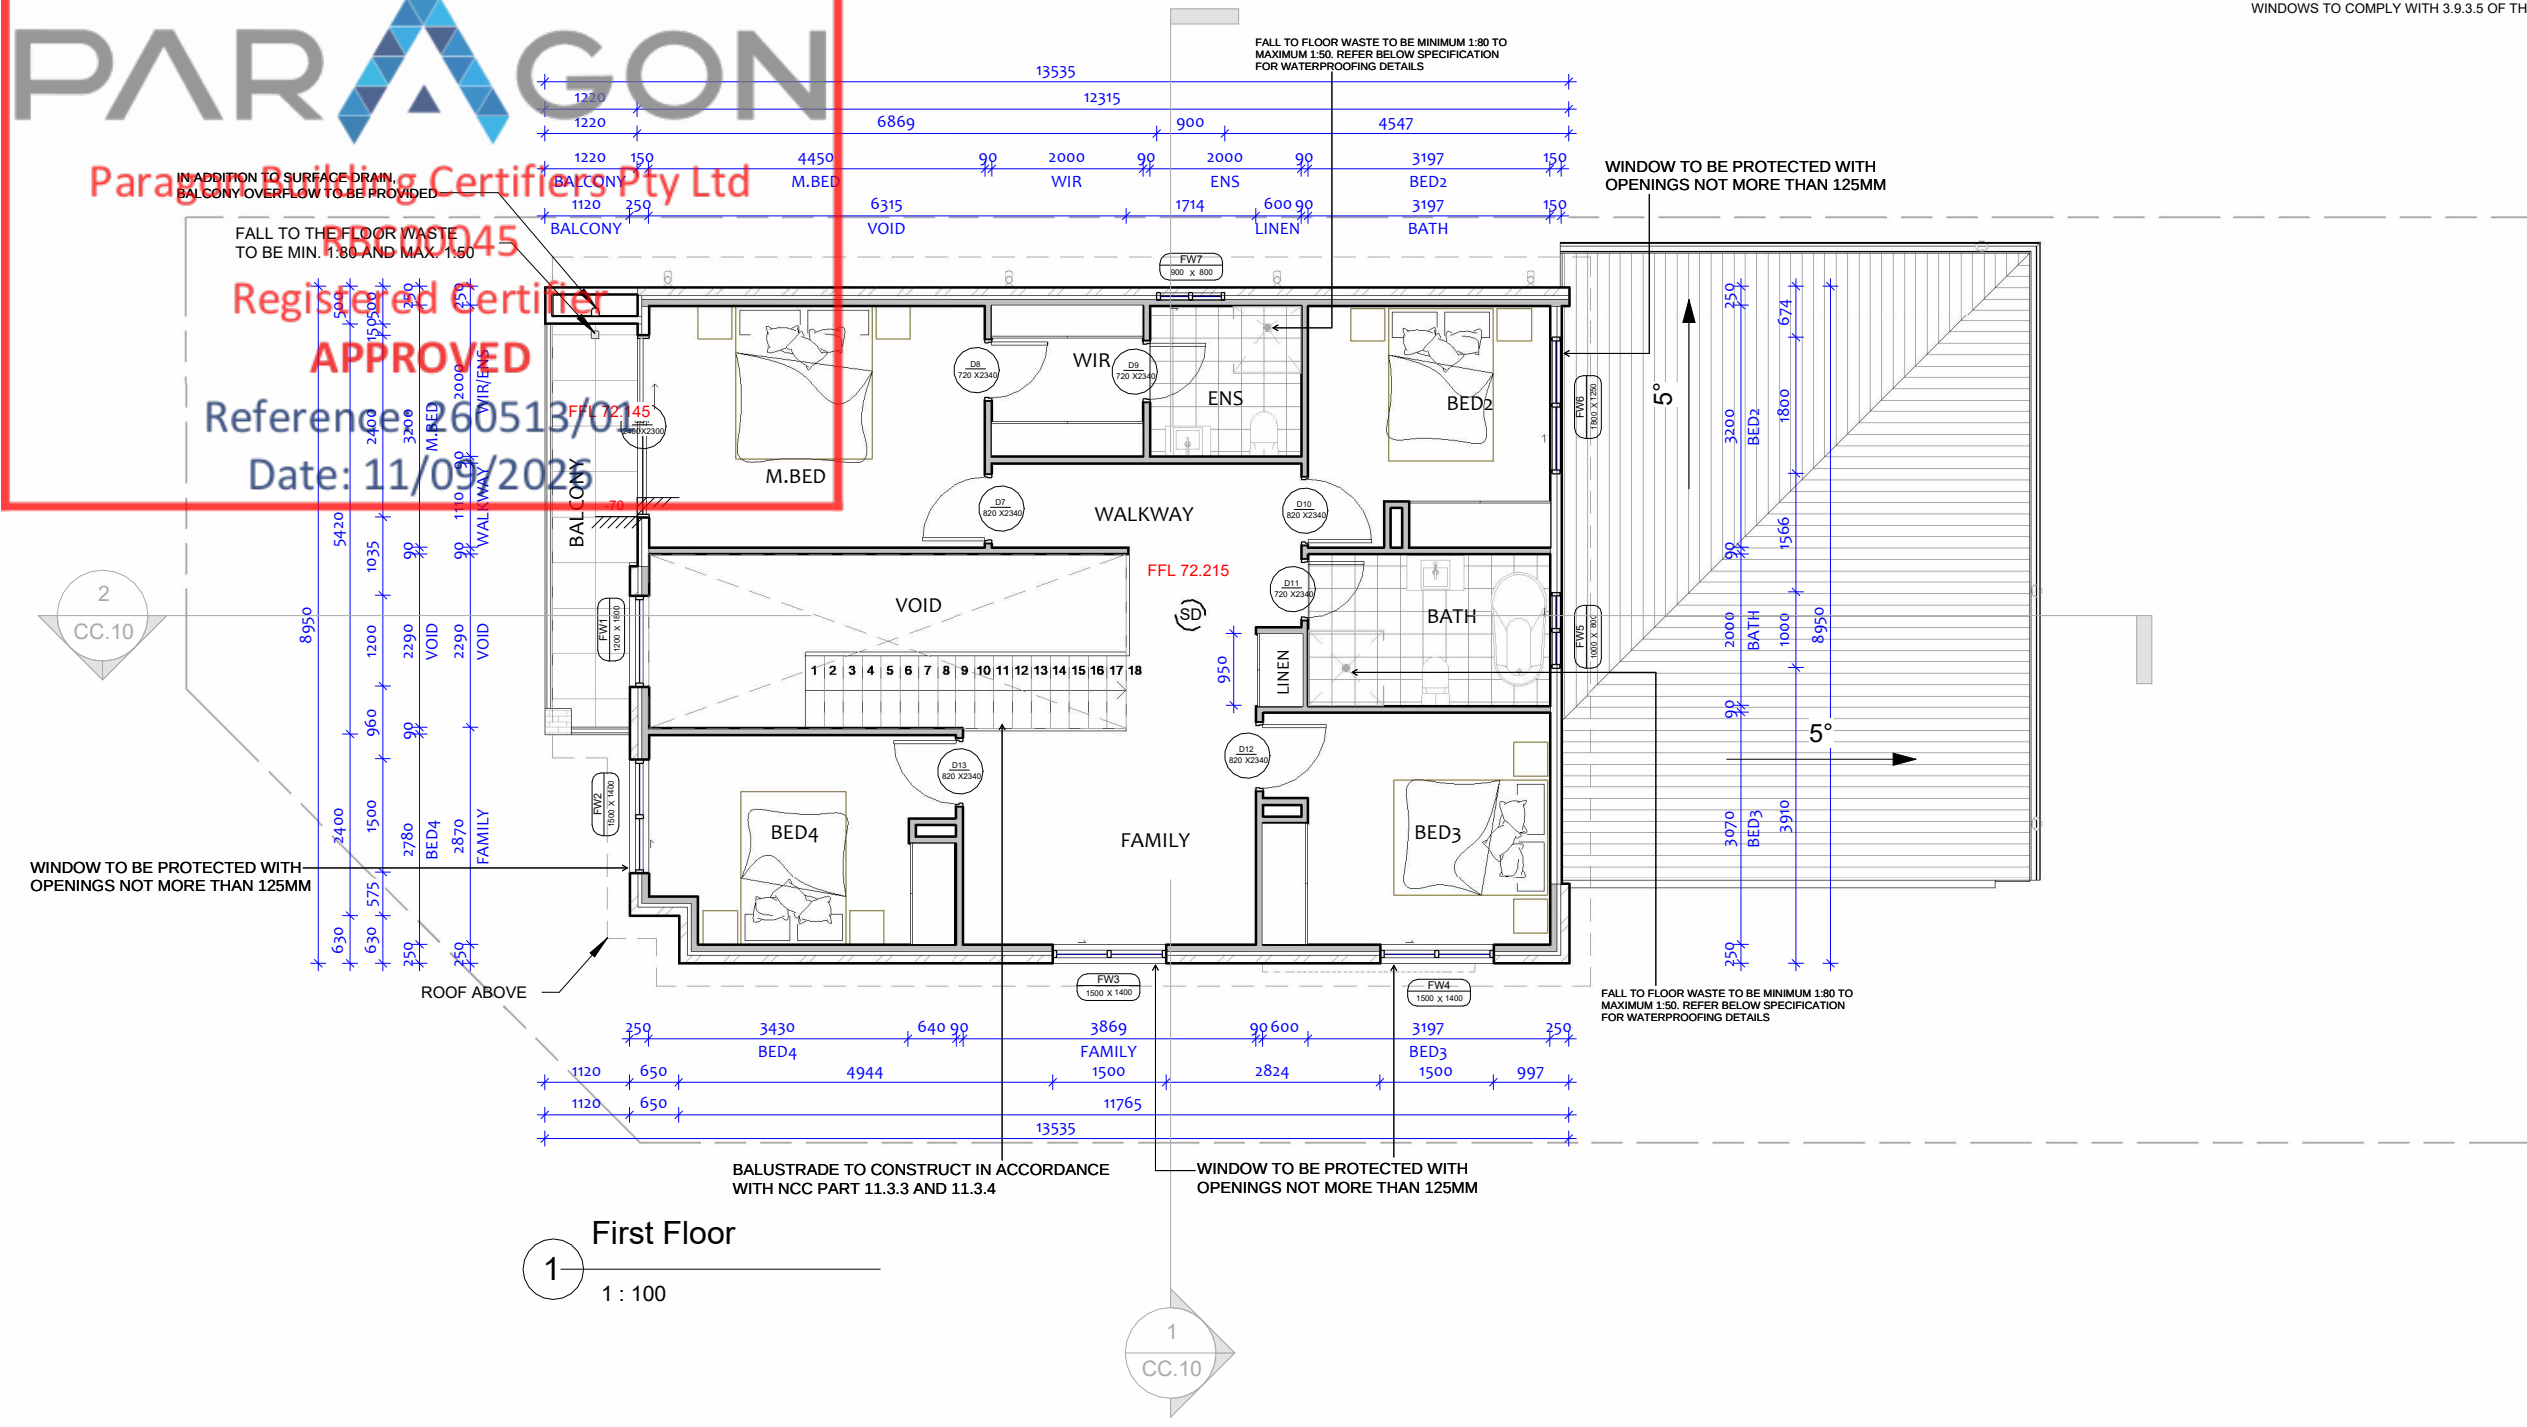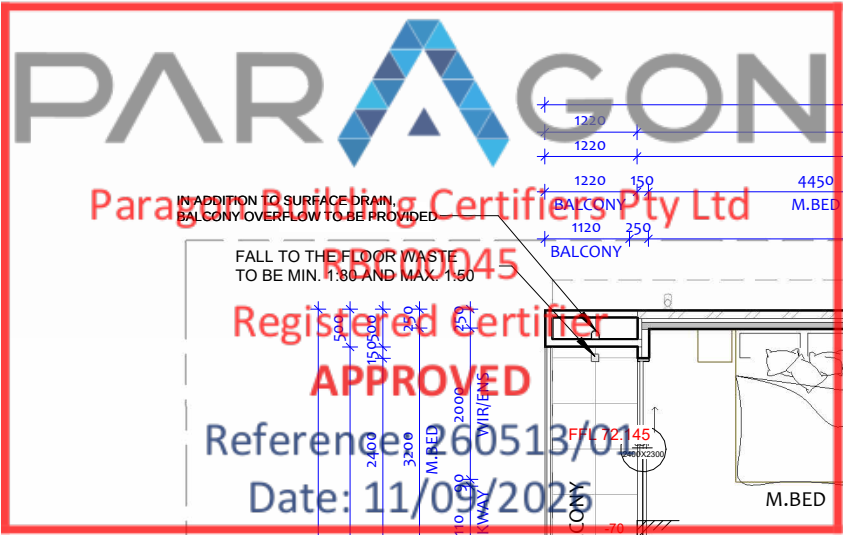

1 First Floor
1 : 100

NOTE: PLEASE REFER TO TENDER FOR ALL INCLUSIONS.

REV	DATE	DESCRIPTION	BY
4	7-07-2026	Site Address updated	
3	23-06-2026	DA ISSUE	
2	3-04-2026	Brick column added at balcony - Ek	
1	02-04-2026	Bank Set	




THIS DRAWING IS THE EXCLUSIVE PROPERTY OF THE DEVELOPER & THE REPRODUCTION OF ANY PART WITHOUT THE PRIOR WRITTEN CONSENT OF THE DEVELOPER IS A VIOLATION OF APPLICABLE LAWS. IN NO EVENT SHALL THE DEVELOPER BE HELD LIABLE FOR SPECIAL COLLATERAL, INCIDENTAL OR CONSEQUENTIAL LIABILITY IN CONNECTION WITH THE USE OF THIS DIGITAL DATA ONCE RELEASED FROM THE DEVELOPER'S OFFICE. THIS DRAWING IS TO BE READ & UNDERSTOOD IN CONJUNCTION WITH THE STRUCTURAL, MECHANICAL, ELECTRICAL & / OR ANY OTHER CONSULTANT'S DOCUMENTATION AS MAY BE APPLICABLE TO THE PROJECT PRIOR TO THE START OF ANY WORKS AND FOR ITS DURATION.


PROJECT:
46 Gunyadu Street

Lot 520 in Dp 1310900 at 46 Gunyadu Street Austral NSW 2179

DRAWING TITLE:
FIRST FLOOR LEVEL

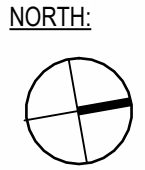

CC ISSUE			
LOT NO:	DATE:	SCALE:	DRAWING No:
520	7-09-2026	1 : 100	CC.06
DRAWN BY:	CHECKED BY:		ISSUED BY:
AS	RH		
DRAFTED BY:	CLIENT NAME:		
SL	Anushka Gartaula Siwakoti		

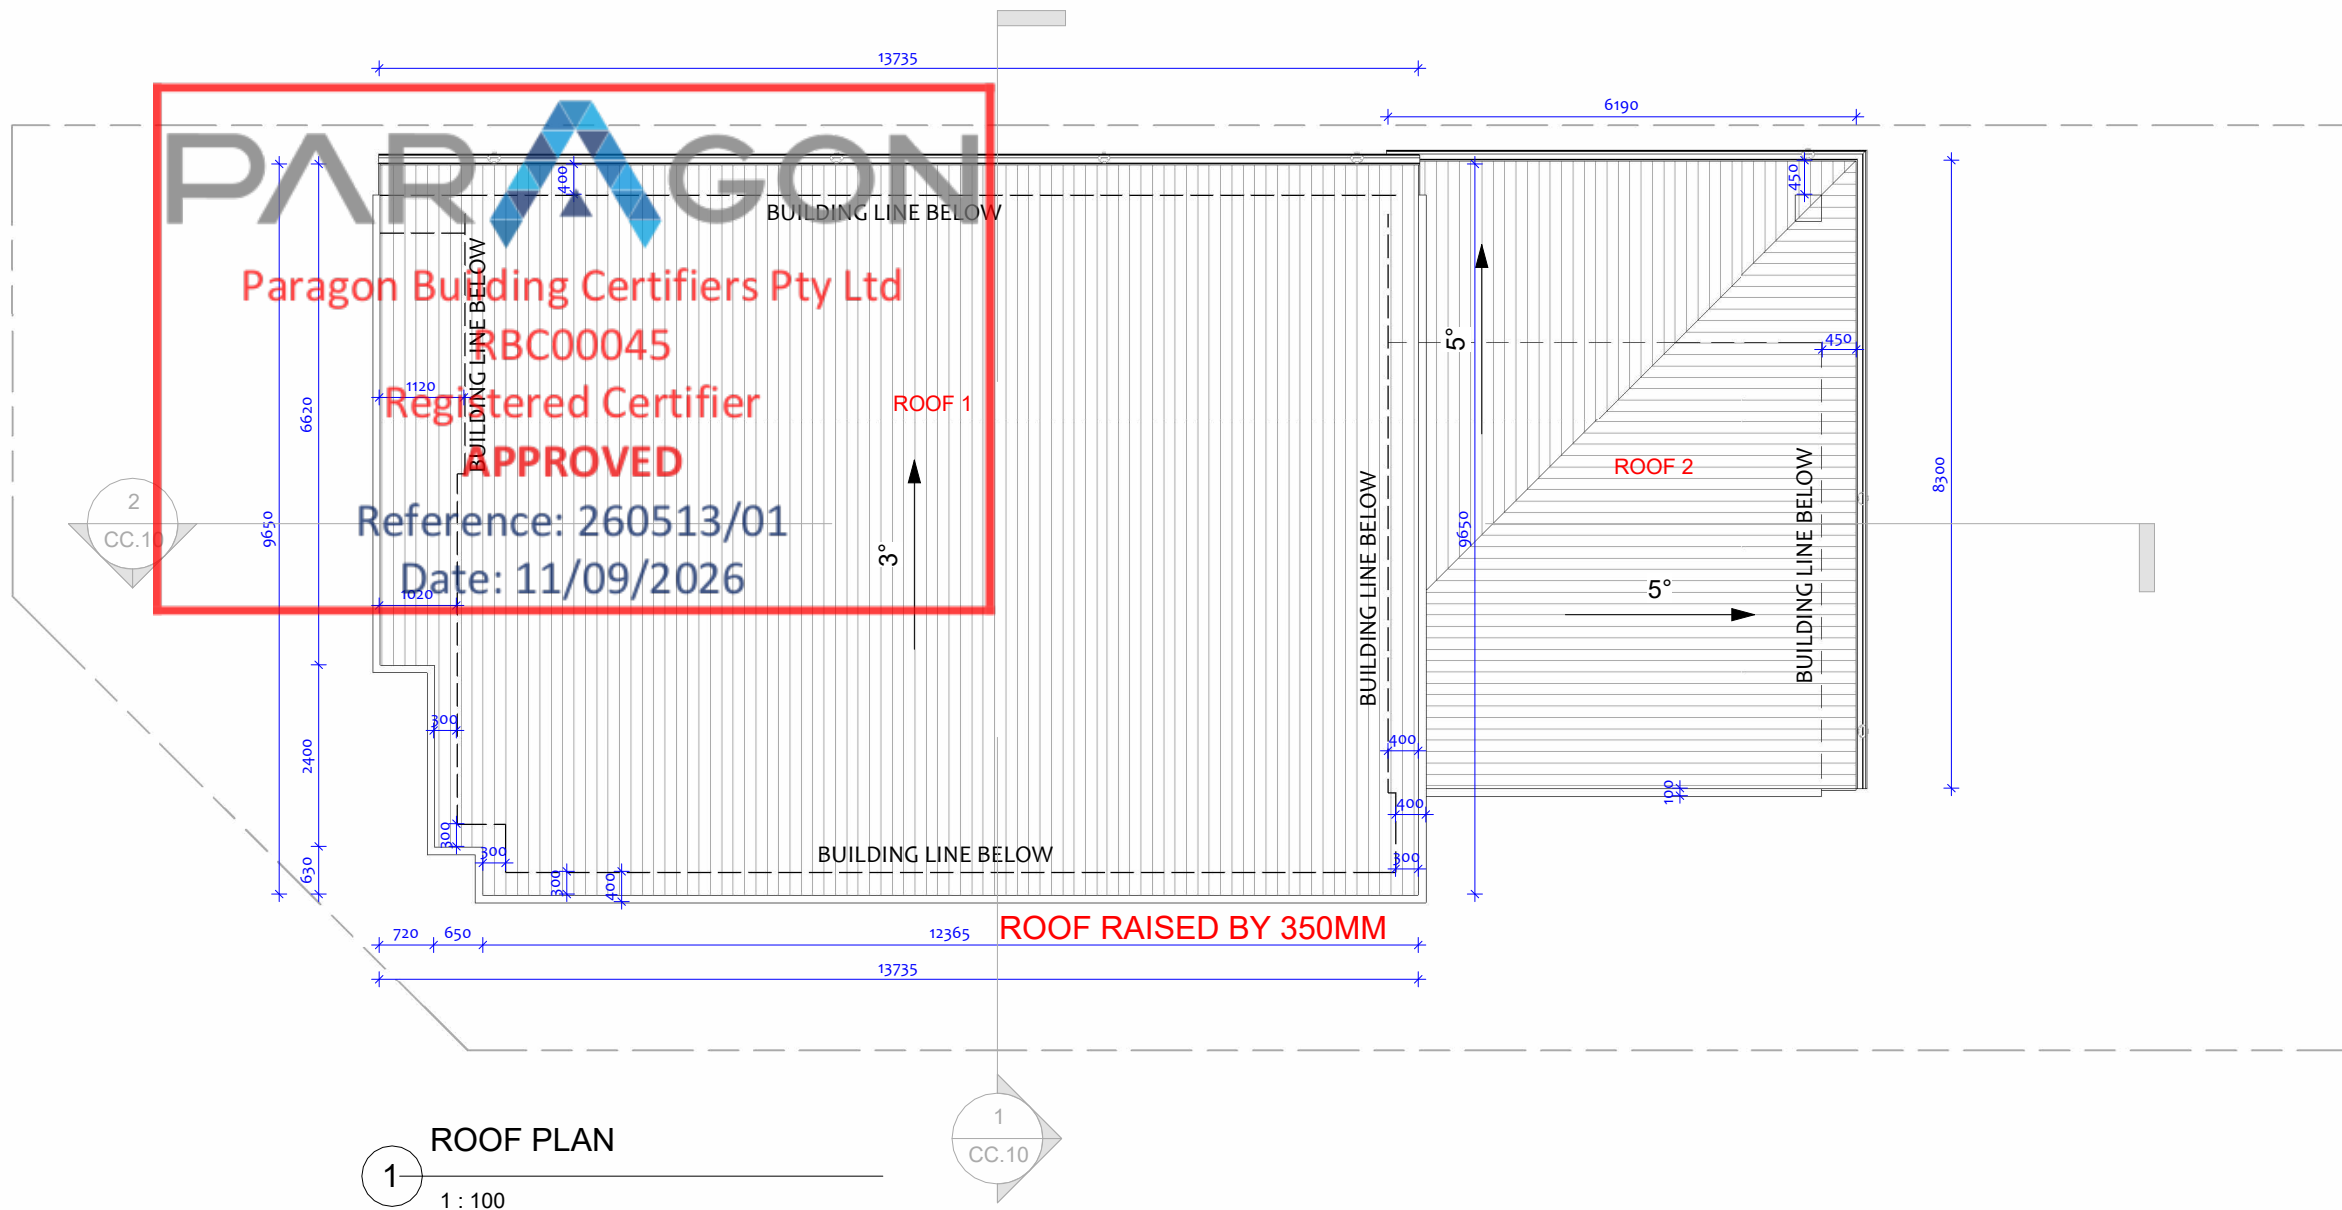

IMPORTANT NOTES:
ALL DIMENSIONS AND NOTES ON ALL PLANS MUST BE CHECKED AND VERIFIED BY BUILDERS AND OWNER PRIOR TO COMMENCEMENT OF ANY BUILDING WORKS. TO CLARIFY AND CONFIRM WITH CONSTRUCTION COMPANY FOR DISCREPANCIES ON ALL DOCUMENTS AND PLANS PROVIDED FOR CONSTRUCTION. ANY WORK INDICATED ON THE PLAN BUT NOT IN THE SPECIFICATION BUT WHICH IS NECESSARY AS PART OF THE CONTRACT, VARIATION TO PLANS, SPECIFICATIONS MAY NOT BE MADE WITHOUT THE WRITTEN CONSENT OF OWNER. IT IS THE RESPONSIBILITY OF THE BUILDER/END USER TO VERIFY PLANS AND SPECIFICATIONS AS TO THEIR ACCURACY AND COMPLY CURRENT BCA AND AUSTRALIAN STANDARDS. WINDOWS TO COMPLY WITH 3.9.3.5 OF THE BCA.

ABCB HOUSING PROVISIONS STANDARD 2022

10.8.3 VENTILATION OF ROOF SPACES

1. IN CLIMATE ZONES 6,7 AND 8, A ROOF MUST HAVE A ROOF SPACE THAT
- (A) IS LOCATED
- (I) IMMEDIATELY ABOVE THE *PRIMARY INSULATION LAYER*, OR
 - (II) IMMEDIATELY ABOVE SARKING WITH A *VAPOUR PERMEANCE* OF NOT LESS THAN 1.14 $\mu\text{g}/\text{m}^2\text{s}$, WHICH IS IMMEDIATELY ABOVE THE *PRIMARY INSULATION LAYER*, OR
 - (III) IMMEDIATELY ABOVE CEILING INSULATION THAT MEETS THE REQUIREMENTS OF 13.2.3(3) AND 13.2.3(4); AND
- (B) HAS A HEIGHT OF NOT LESS THAN 20MM; AND
- (C) IS EITHER -
- (I) VENTILATED TO OUTDOOR AIR THROUGH EVENLY DISTRIBUTED OPENINGS IN ACCORDANCE WITH TABLE 10.8.3; OR
 - (II) LOCATED IMMEDIATELY UNDERNEATH THE ROOF TILES OF A UNSARKED TILED ROOF.

Figure 7.2.3:

Minimum pitch requirements for metal roofing profiles

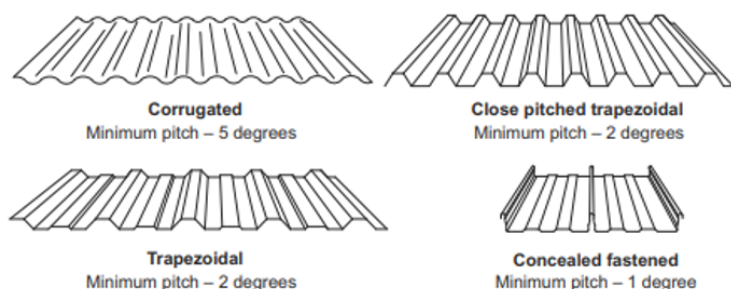


Figure 10.8.3 (explanatory): Example of roof space with low level ventilation

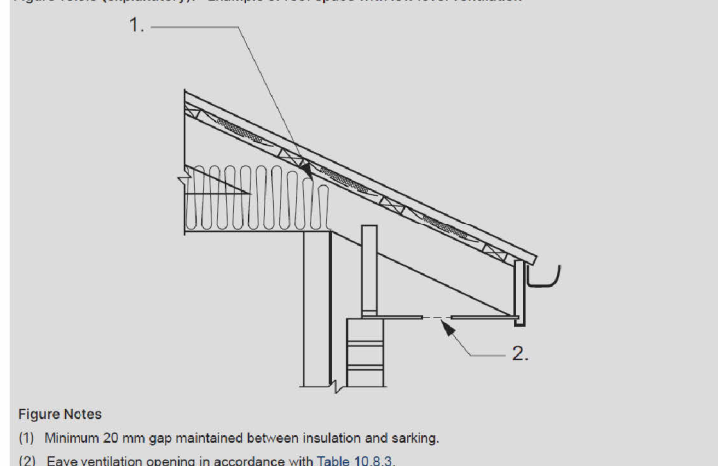


Figure Notes
(1) Minimum 20 mm gap maintained between insulation and sarking.
(2) Eave ventilation opening in accordance with Table 10.8.3.

Table 10.8.3: Roof space ventilation requirements

Roof pitch	Ventilation openings
< 10°	25,000 mm ² /m provided at each of two opposing ends
≥ 10° and < 15°	25,000 mm ² /m provided at the eaves and 5,000 mm ² /m at high level
≥ 15° and < 75°	7,000 mm ² /m provided at the eaves and 5,000 mm ² /m at high level, plus an additional 18,000 mm ² /m at the eaves if the roof has a cathedral ceiling

Roof Schedule

Mark	Base Level	Area	Comments
ROOF2	First Floor	52 m ²	COLORBOND
ROOF 1	CEILING LEVEL	130 m ²	COLORBOND
Grand total: 2		182 m ²	

CC ISSUE

REV	DATE	DESCRIPTION	BY
4	7-07-2026	Site Address updated	
3	23-06-2026	DA ISSUE	


RUBY HOMES

THIS DRAWING IS THE EXCLUSIVE PROPERTY OF THE DEVELOPER & THE REPRODUCTION OF ANY PART WITHOUT THE PRIOR WRITTEN CONSENT OF THE DEVELOPER IS A VIOLATION OF APPLICABLE LAWS. IN NO EVENT SHALL THE DEVELOPER BE HELD LIABLE FOR SPECIAL COLLATERAL, INCIDENTAL OR CONSEQUENTIAL LIABILITY IN CONNECTION WITH THE USE OF THIS DIGITAL DATA ONCE RELEASED FROM THE DEVELOPER'S OFFICE. THIS DRAWING IS TO BE READ & UNDERSTOOD IN CONJUNCTION WITH THE STRUCTURAL, MECHANICAL, ELECTRICAL & / OR ANY OTHER CONSULTANT'S DOCUMENTATION AS MAY BE APPLICABLE TO THE PROJECT PRIOR TO THE START OF ANY WORKS AND FOR ITS DURATION.


PROJECT:
46 Gunyadu Street

Lot 520 in Dp 1310900 at 46 Gunyadu Street Austral NSW 2179


DRAWING TITLE:
ROOF PLAN

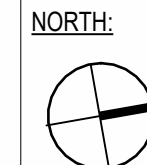

LOT NO:	DATE:	SCALE:	DRAWING No:	REV:
520	7-09-2026	1 : 100	CC.07	4
DRAWN BY:	CHECKED BY:	DRAFTED BY:	CLIENT NAME:	ISSUED BY:
AS	RH	SL	Anushka Gartaula Siwakoti	

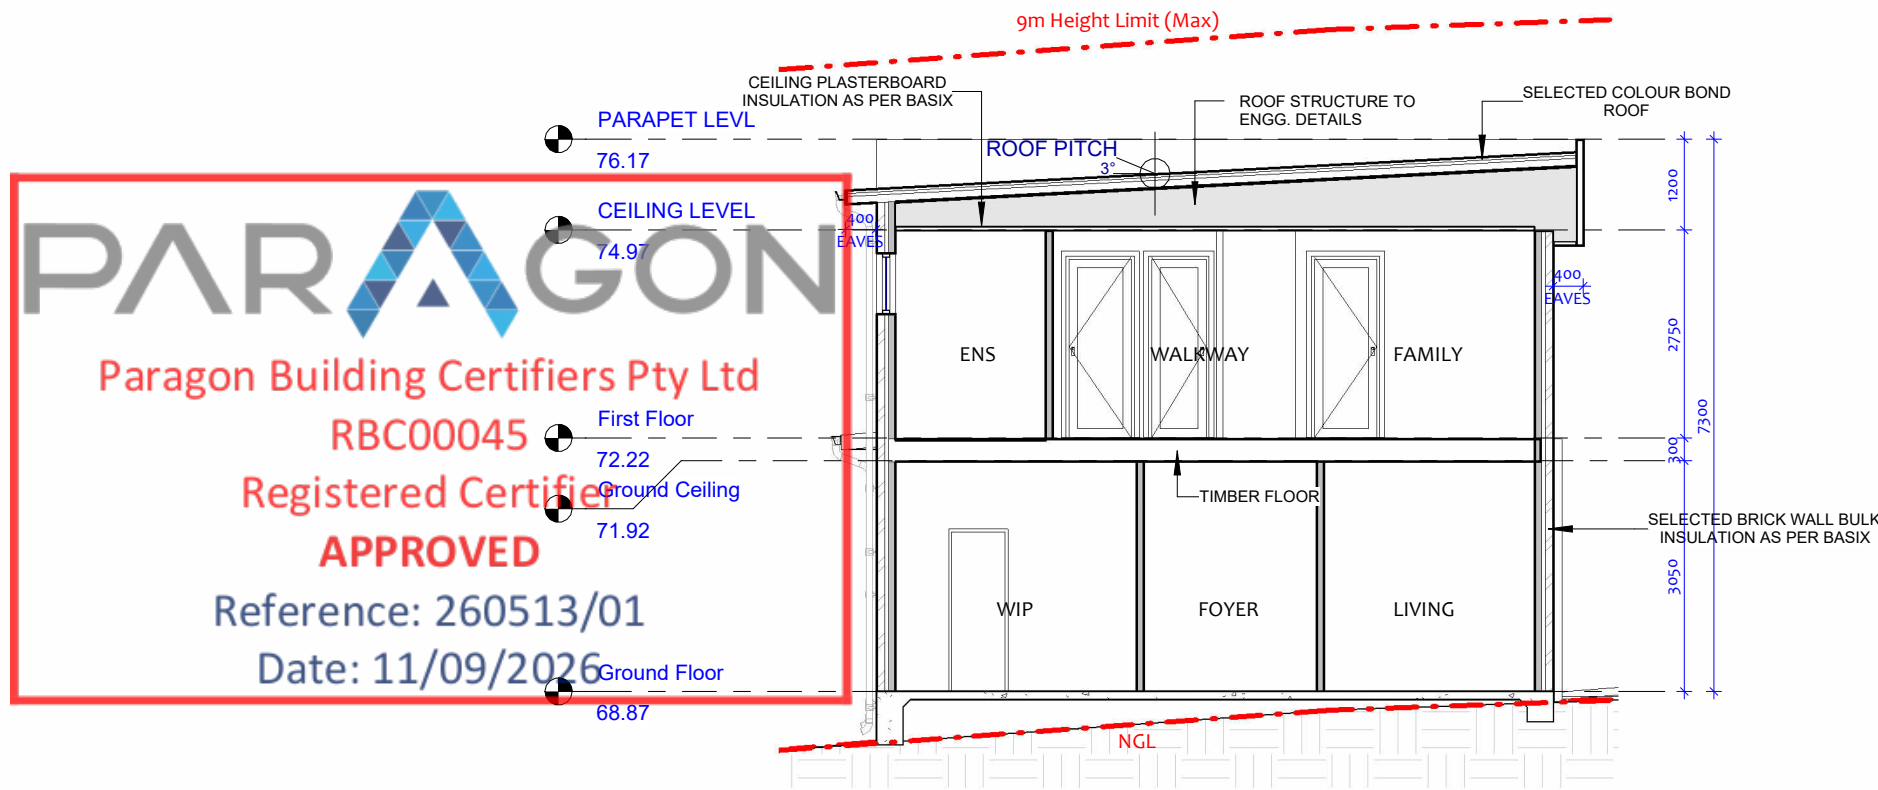

1 CROSS SECTION
1 : 100

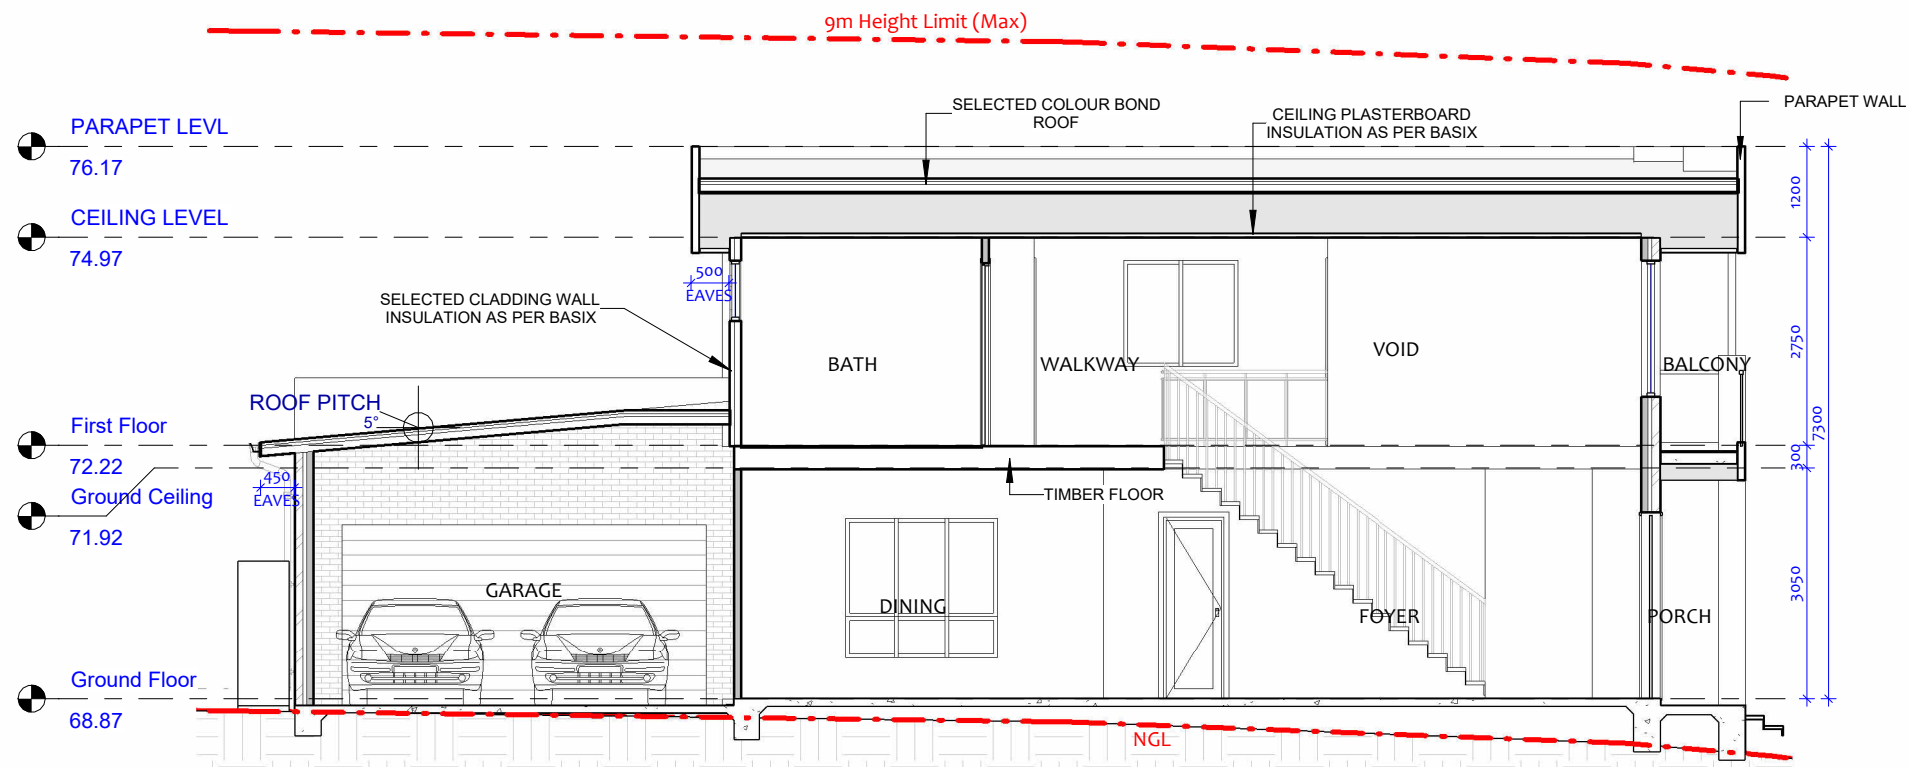

2 LONGITUDINAL SECTION
1 : 100

REV	DATE	DESCRIPTION	BY
4	7-07-2026	Site Address updated	
3	23-06-2026	DA ISSUE	


RUBY HOMES

THIS DRAWING IS THE EXCLUSIVE PROPERTY OF THE DEVELOPER & THE REPRODUCTION OF ANY PART WITHOUT THE PRIOR WRITTEN CONSENT OF THE DEVELOPER IS A VIOLATION OF APPLICABLE LAWS. IN NO EVENT SHALL THE DEVELOPER BE HELD LIABLE FOR SPECIAL COLLATERAL, INCIDENTAL OR CONSEQUENTIAL LIABILITY IN CONNECTION WITH THE USE OF THIS DIGITAL DATA ONCE RELEASED FROM THE DEVELOPER'S OFFICE. THIS DRAWING IS TO BE READ & UNDERSTOOD IN CONJUNCTION WITH THE STRUCTURAL, MECHANICAL, ELECTRICAL & / OR ANY OTHER CONSULTANT'S DOCUMENTATION AS MAY BE APPLICABLE TO THE PROJECT PRIOR TO THE START OF ANY WORKS AND FOR ITS DURATION.


PROJECT:
46 Gunyadu Street

Lot 520 in Dp 1310900 at 46
Gunyadu Street Austral NSW 2179

DRAWING TITLE:
SECTIONS

NORTH:

CC ISSUE					
LOT NO:	DATE:	SCALE:	DRAWING No:	REV:	
520	7-09-2026	1 : 100	CC.10	4	
DRAWN BY:	CHECKED BY:			ISSUED BY:	
AS	RH				
DRAFTED BY:	CLIENT NAME:				
SL	Anushka Gartaula Siwakoti				

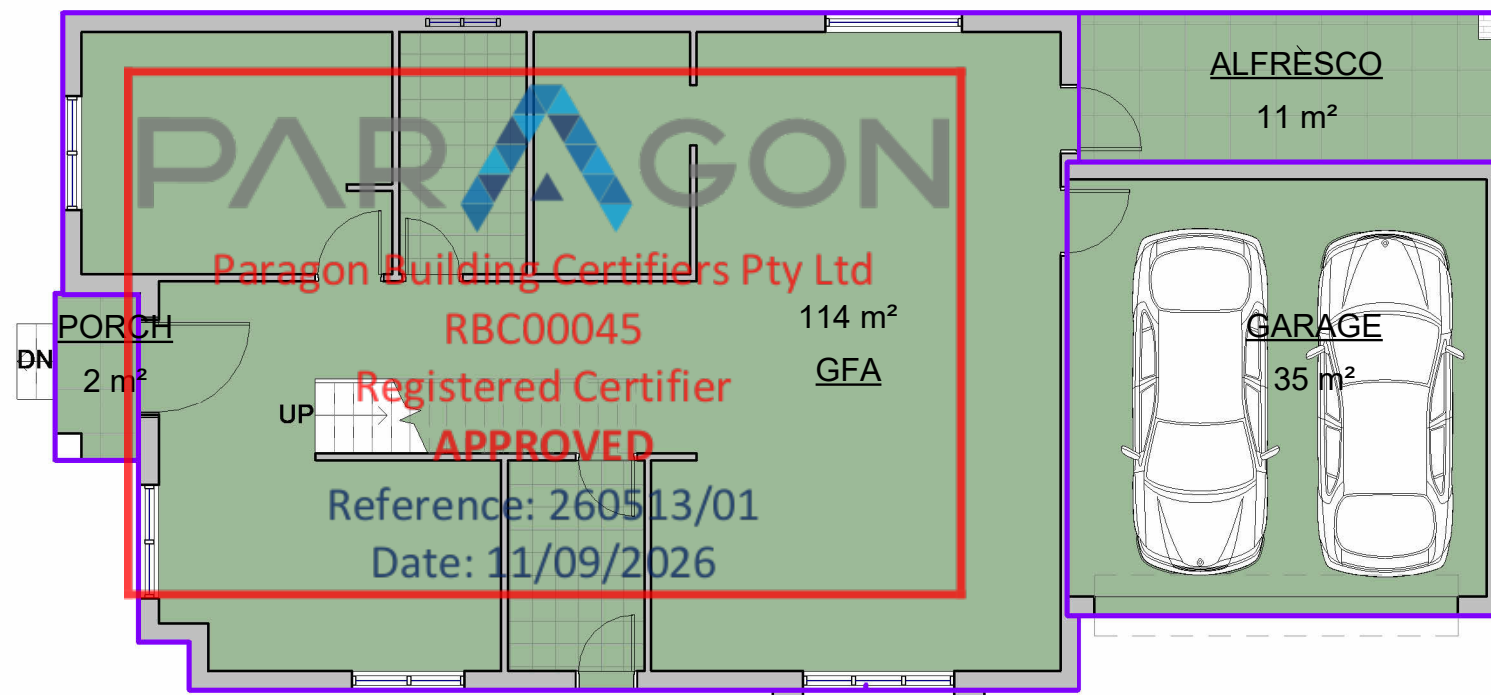

1 Ground Floor
1 : 100

GROUND COVERAGE(BUILT UP)	
Name	Area

Ground Floor

GFA	114 m ²
PORCH	2 m ²
ALFRESCO	11 m ²
GARAGE	35 m ²


Ground Floor: 4 162 m²

First Floor

FFA	96 m ²
BALCONY	7 m ²
VOID	14 m ²

First Floor: 3 117 m²

Grand total: 7 279 m²

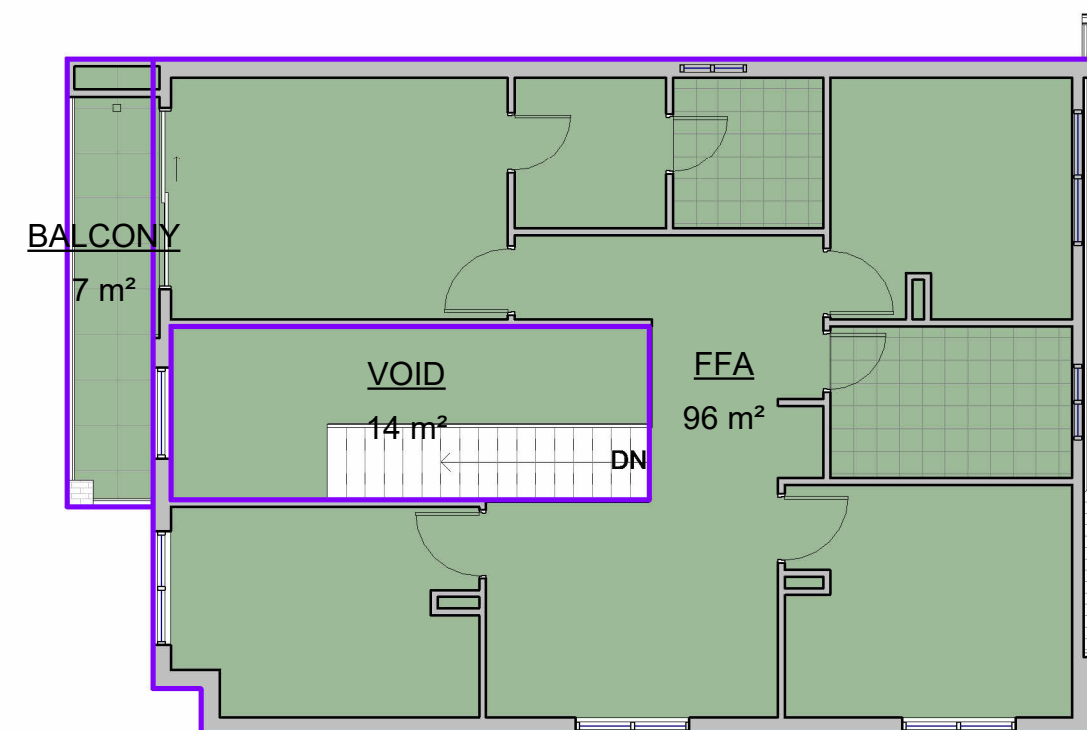

2 First Floor
1 : 100

REV	DATE	DESCRIPTION	BY
4	7-07-2026	Site Address updated	
3	23-06-2026	DA ISSUE	
1	02-04-2026	Bank Set	

PROJECT:
46 Gunyadu Street

Lot 520 in Dp 1310900 at 46
Gunyadu Street Austral NSW 2179


THIS DRAWING IS THE EXCLUSIVE PROPERTY OF THE DEVELOPER & THE REPRODUCTION OF ANY PART WITHOUT THE PRIOR WRITTEN CONSENT OF THE DEVELOPER IS A VIOLATION OF APPLICABLE LAWS. IN NO EVENT SHALL THE DEVELOPER BE HELD LIABLE FOR SPECIAL COLLATERAL, INCIDENTAL OR CONSEQUENTIAL LIABILITY IN CONNECTION WITH THE USE OF THIS DIGITAL DATA ONCE RELEASED FROM THE DEVELOPER'S OFFICE. THIS DRAWING IS TO BE READ & UNDERSTOOD IN CONJUNCTION WITH THE STRUCTURAL, MECHANICAL, ELECTRICAL & / OR ANY OTHER CONSULTANT'S DOCUMENTATION AS MAY BE APPLICABLE TO THE PROJECT PRIOR TO THE START OF ANY WORKS AND FOR ITS DURATION.

DRAWING TITLE: BUILT UP AREA

NORTH:

LOT NO: 520	DATE: 7-09-2026	SCALE: 1 : 100	DRAWING No: CC.11	REV: 4
DRAWN BY: AS	CHECKED BY: RH			ISSUED BY:
DRAFTED BY: SL	CLIENT NAME: Anushka Gartaula Siwakoti			

CC ISSUE

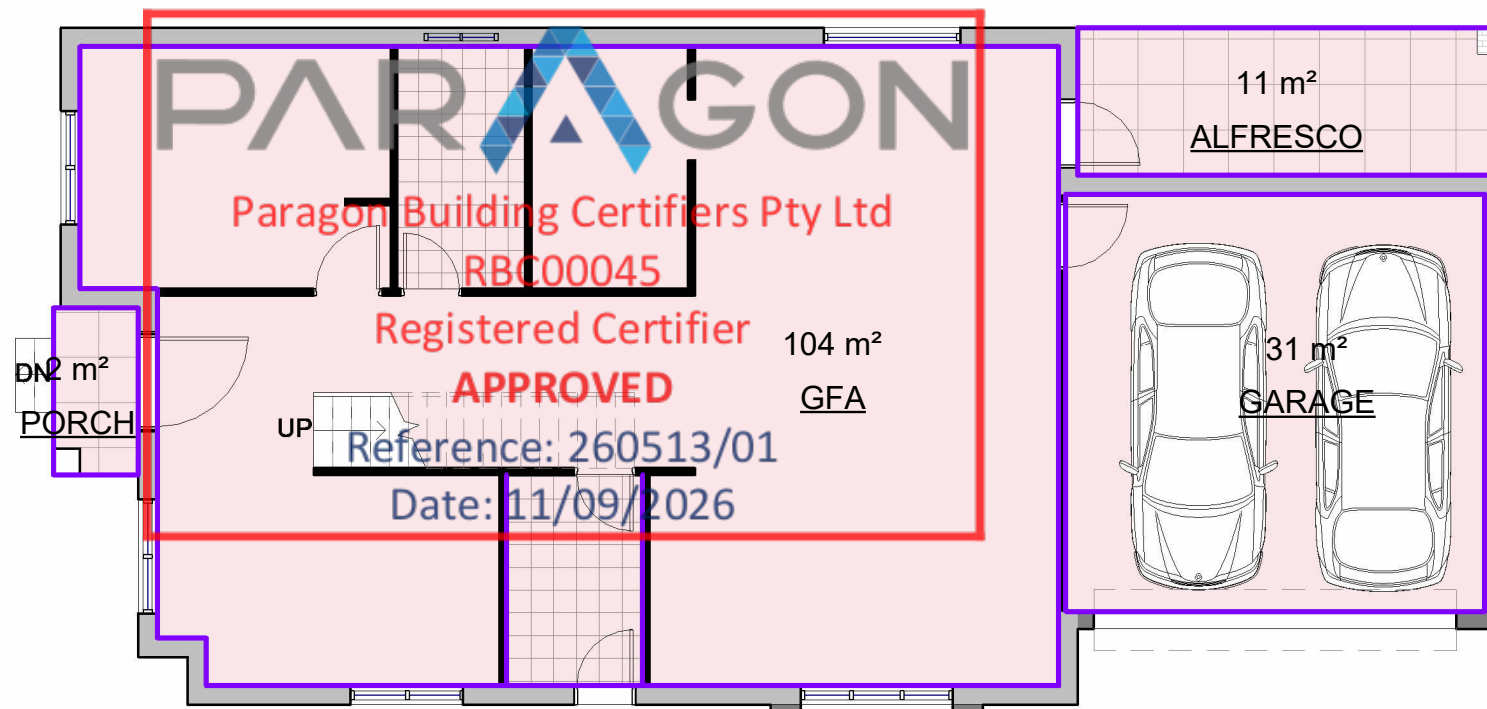

Area Schedule (Rentable)	
Name	Area

Ground Floor

GFA	104 m ²
GARAGE	31 m ²
ALFRESCO	11 m ²
PORCH	2 m ²

Ground Floor: 4 148 m²


First Floor

FFA	86 m ²
STAIRCASE/VOID	14 m ²
BALCONY	6 m ²

First Floor: 3 107 m²

Grand total: 7 254 m²

1 Ground Floor
1 : 100

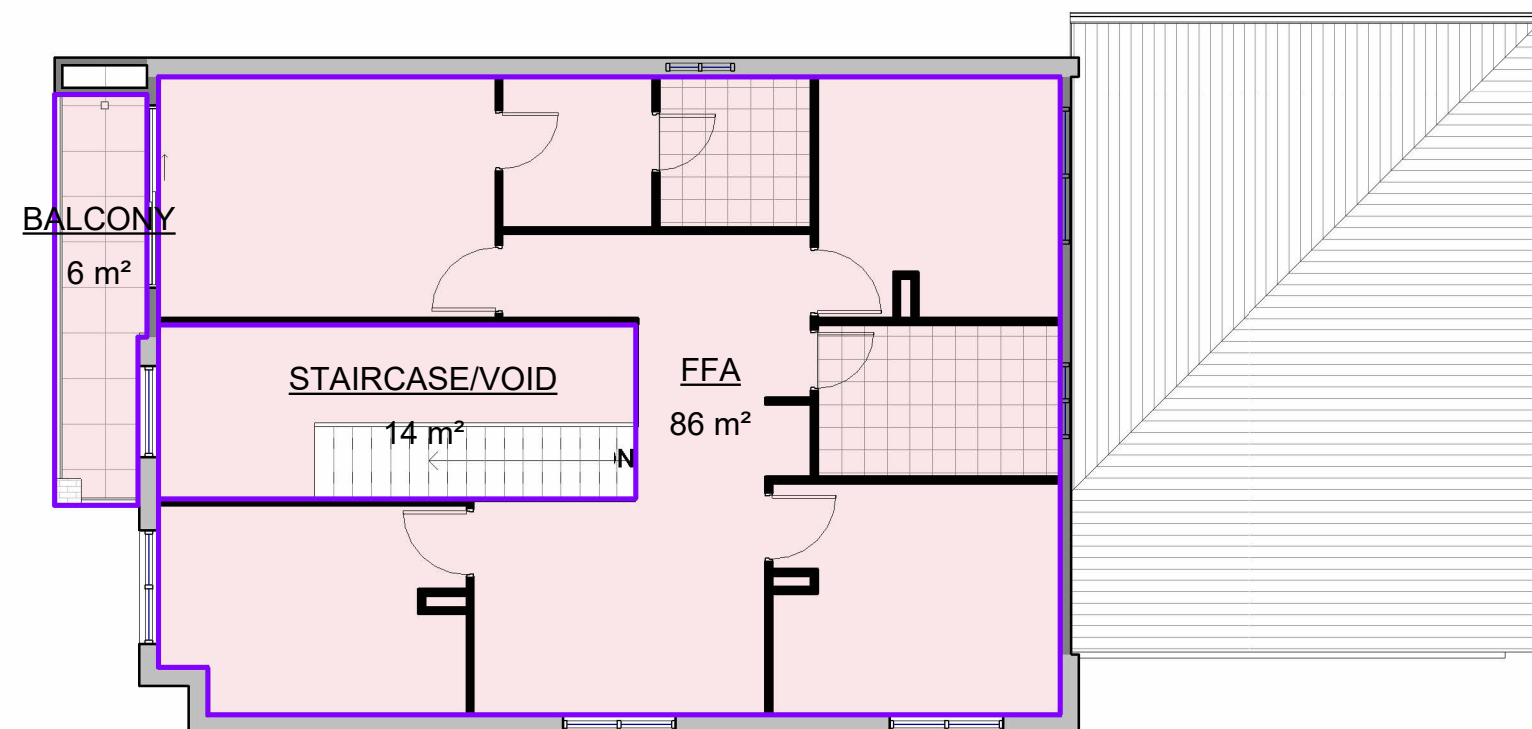

2 First Floor
1 : 100


REV	DATE	DESCRIPTION	BY
4	7-07-2026	Site Address updated	
3	23-06-2026	DA ISSUE	



THIS DRAWING IS THE EXCLUSIVE PROPERTY OF THE DEVELOPER & THE REPRODUCTION OF ANY PART WITHOUT THE PRIOR WRITTEN CONSENT OF THE DEVELOPER IS A VIOLATION OF APPLICABLE LAWS. IN NO EVENT SHALL THE DEVELOPER BE HELD LIABLE FOR SPECIAL COLLATERAL, INCIDENTAL OR CONSEQUENTIAL LIABILITY IN CONNECTION WITH THE USE OF THIS DIGITAL DATA ONCE RELEASED FROM THE DEVELOPER'S OFFICE. THIS DRAWING IS TO BE READ & UNDERSTOOD IN CONJUNCTION WITH THE STRUCTURAL, MECHANICAL, ELECTRICAL & / OR ANY OTHER CONSULTANT'S DOCUMENTATION AS MAY BE APPLICABLE TO THE PROJECT PRIOR TO THE START OF ANY WORKS AND FOR ITS DURATION.

PROJECT:
46 Gunyadu Street
 Lot 520 in Dp 1310900 at 46
 Gunyadu Street Austral NSW 2179

DRAWING TITLE:
RENTABLE AREA
PLAN

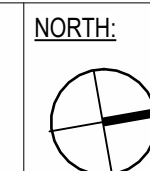

LOT NO:	DATE:	SCALE:	DRAWING No:	REV:
520	7-09-2026	1 : 100	CC.12	4
DRAWN BY:	CHECKED BY:			ISSUED BY:
AS	RH			
DRAFTED BY:	CLIENT NAME:			
SL	Anushka Gartaula Siwakoti			

CC ISSUE



Paragon Building Certifiers Pty Ltd

RBC00045

Registered Certifier

APPROVED


Reference: 260513/01

Date: 11/09/2026



1.RF

Manufacturer: Colorbond®
Range:Mini ORB
Finish : Shale Grey
or Similar

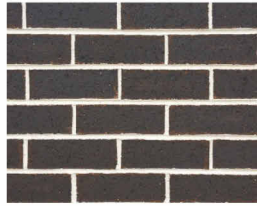

2. BR1

Manufacturer:Austral Bricks
Range:Wilderness Design
Colour Details:Blackbutt
Code:SKU 410750021420000328100
or Similar



3. CR1

Manufacturer:Austral Bricks
Range:Everyday Life Engage
Colour Details:Engage
Code:SKU 210250011130000301100
or Similar




4. CD1

Manufacturer: JamesHardie
Range:Weatherboard
Product Details:Hardie Plank
Smooth Finish
Finish : Paint Finish (Taubmans -
Opulent White or Similar white and
Neutral colour)




5. AL

Windows and Sliding Door
Manufacturer: ABM Door & Window
Finish : Monument

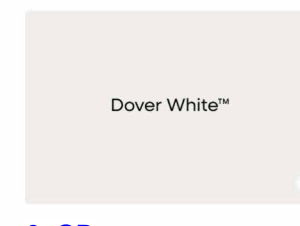

6. GD

Manufacturer: Door Works
Range:Flat Panel
Product Details:Colorbond® is
a high-quality, pre-painted
steel product
Finish : Woodgrain Colorbond-
Dover White

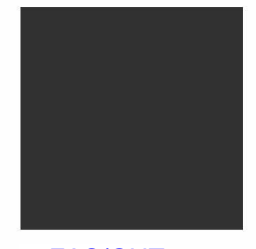

7. FAS/GUT

Gutter fascia,gutter
Manufacturer: Colorbond®
Finish : Monument

NOTE : ALL COLOURS SPECIFIED ARE INDICATIVE ONLY AND ARE SUBJECT TO VARIATION AND TO AVAILABILITY
ANY DISCREPANCY PLEASE FOLLOW AS PER RENDERED IMAGE

REV	DATE	DESCRIPTION	BY
4	7-07-2026	Site Address updated	
3	23-06-2026	DA ISSUE	



THIS DRAWING IS THE EXCLUSIVE PROPERTY OF THE DEVELOPER & THE REPRODUCTION OF ANY PART WITHOUT THE PRIOR WRITTEN CONSENT OF THE DEVELOPER IS A VIOLATION OF APPLICABLE LAWS. IN NO EVENT SHALL THE DEVELOPER BE HELD LIABLE FOR SPECIAL COLLATERAL, INCIDENTAL OR CONSEQUENTIAL LIABILITY IN CONNECTION WITH THE USE OF THIS DIGITAL DATA ONCE RELEASED FROM THE DEVELOPER'S OFFICE. THIS DRAWING IS TO BE READ & UNDERSTOOD IN CONJUNCTION WITH THE STRUCTURAL, MECHANICAL, ELECTRICAL & / OR ANY OTHER CONSULTANT'S DOCUMENTATION AS MAY BE APPLICABLE TO THE PROJECT PRIOR TO THE START OF ANY WORKS AND FOR ITS DURATION.

PROJECT:
46 Gunyadu Street


Lot 520 in Dp 1310900 at 46
Gunyadu Street Austral NSW 2179

DRAWING TITLE:
COLOR SCHEDULE

NORTH:

LOT NO:	DATE:	SCALE:	DRAWING No:	REV:
520	7-09-2026		CC.14	4
DRAWN BY:	CHECKED BY:	ISSUED BY:		
AS	RH			
DRAFTED BY:	CLIENT NAME:			
SL	Anushka Gartaula Siwakoti			

CC ISSUE

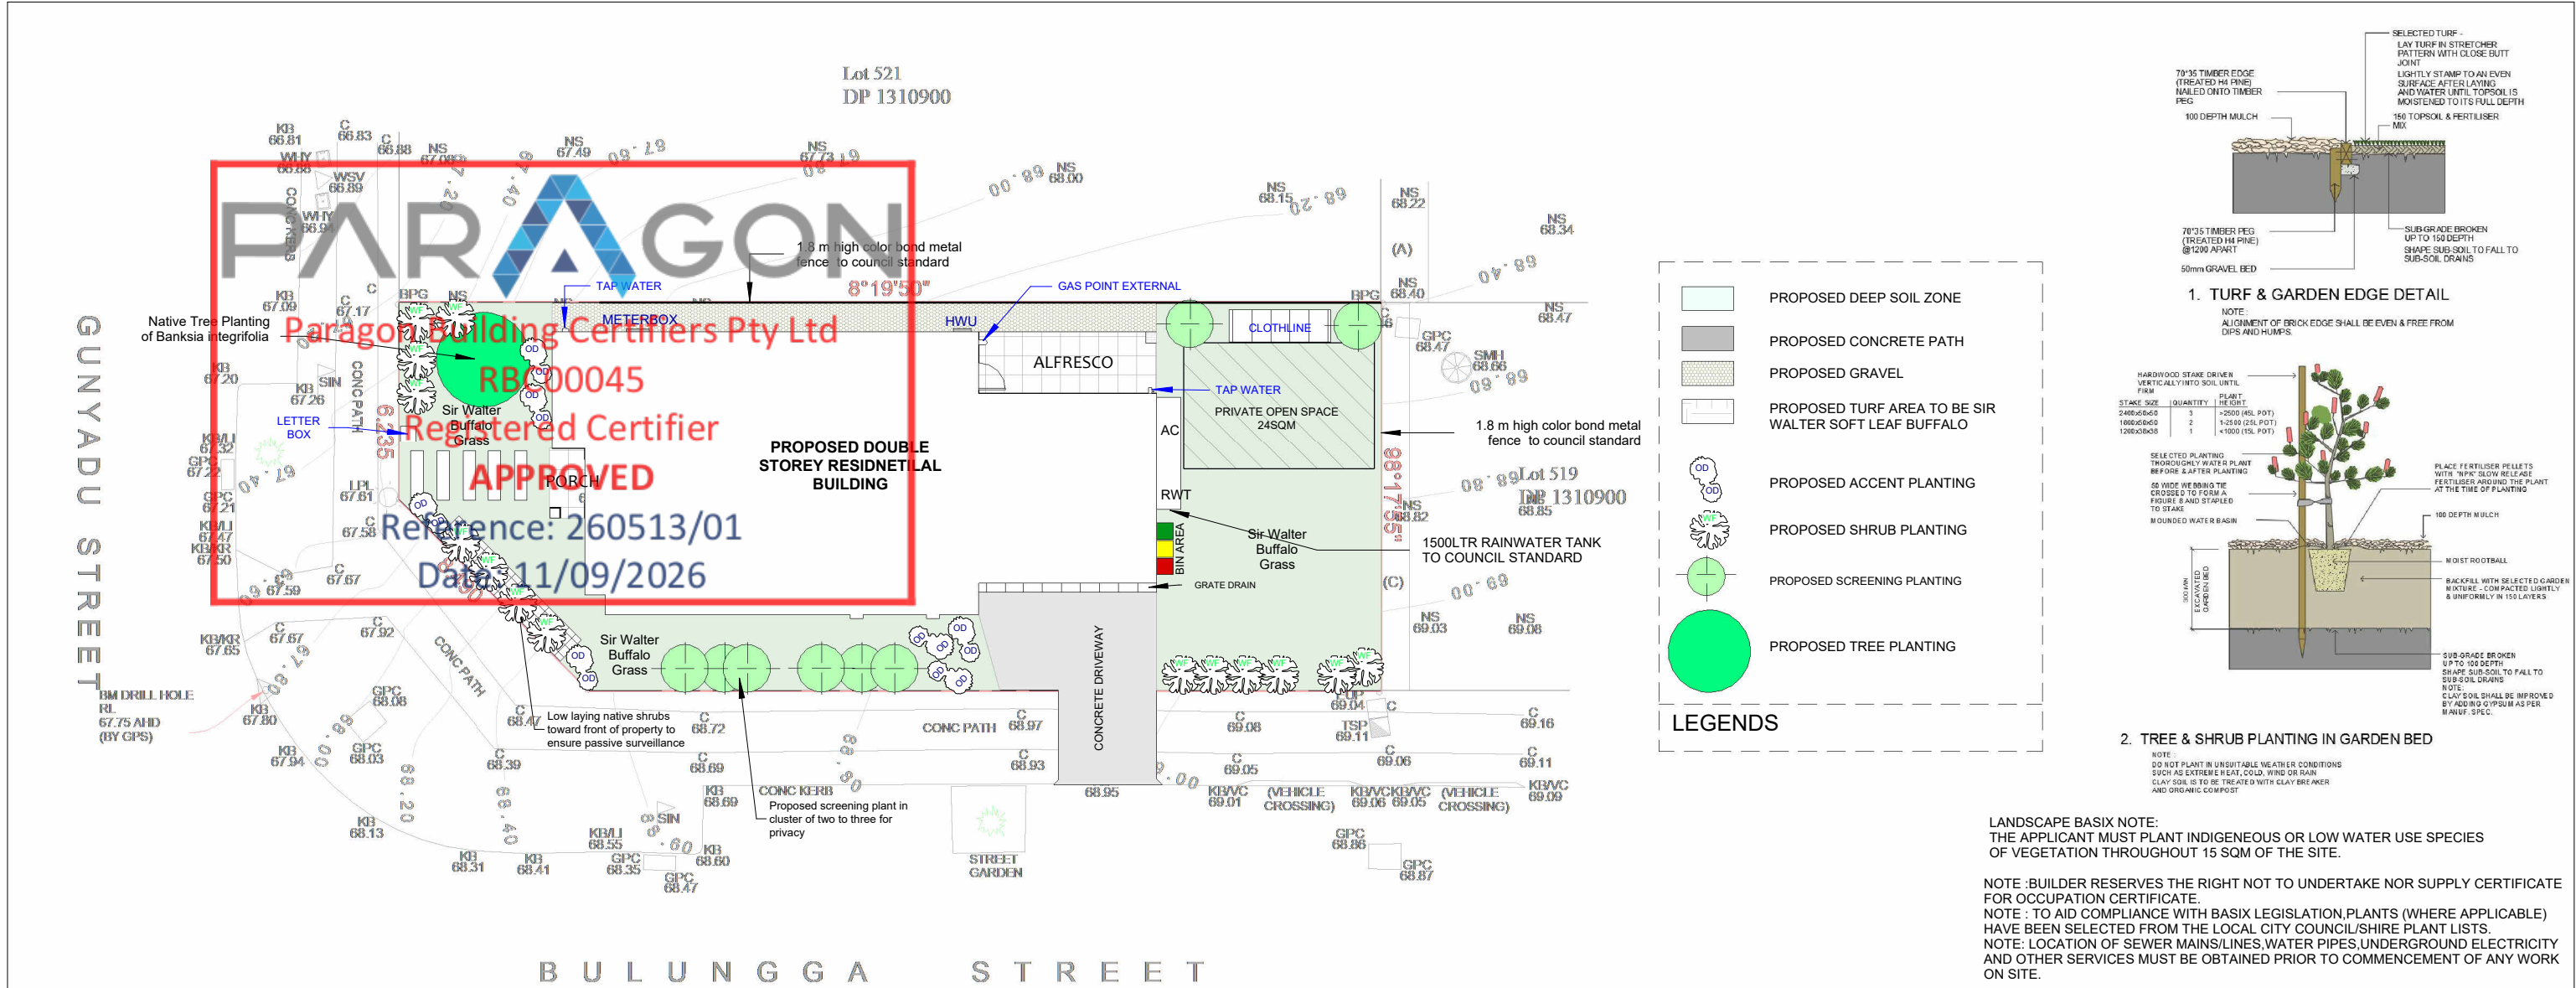

PLANT SCHEDULE

Genus	Common Name	Qty	Pot size	Height	width
Trees					
Banksia integrifolia	coast banksia	1	45L	7	4
Cupaniopsis anacardioides	Tuckeroo	1	45L	8	4
Shrubs					
Grevillea 'moonlight'	Grevillea Moonlight	-	140mm	3	1.5
Leptospermum 'Cardwell'	Tea Tree	-	140mm	1.5	1
Leucophyta Brownii	Cushion Bush	-	140mm	1.5	1
Westringia Fruticosa	Coastal Rosemary	-	140mm	1.5	2
Accents					
Agave Americana	American Aloe	-	200mm	1.5	1.5

LANDSCAPE AREA

FRONT AREA	76.3 m ²
REAR AREA	86 m ²

REV	DATE	DESCRIPTION	BY
4	7-07-2026	Site Address updated	
3	23-06-2026	DA ISSUE	


RUBY HOMES

THIS DRAWING IS THE EXCLUSIVE PROPERTY OF THE DEVELOPER & THE REPRODUCTION OF ANY PART WITHOUT THE PRIOR WRITTEN CONSENT OF THE DEVELOPER IS A VIOLATION OF APPLICABLE LAWS. IN NO EVENT SHALL THE DEVELOPER BE HELD LIABLE FOR SPECIAL COLLATERAL, INCIDENTAL OR CONSEQUENTIAL LIABILITY IN CONNECTION WITH THE USE OF THIS DIGITAL DATA ONCE RELEASED FROM THE DEVELOPER'S OFFICE. THIS DRAWING IS TO BE READ & UNDERSTOOD IN CONJUNCTION WITH THE STRUCTURAL, MECHANICAL, ELECTRICAL & / OR ANY OTHER CONSULTANT'S DOCUMENTATION AS MAY BE APPLICABLE TO THE PROJECT PRIOR TO THE START OF ANY WORKS AND FOR ITS DURATION.

PROJECT:
46 Gunyadu Street

Lot 520 in Dp 1310900 at 46
Gunyadu Street Austral NSW 2179

DRAWING TITLE:
LANDSCAPE PLAN

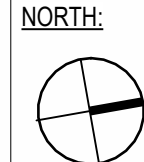

LOT NO: 520	DATE: 7-09-2026	SCALE: 1 : 200	DRAWING No: CC.15	REV: 4
DRAWN BY: AS	CHECKED BY: RH			ISSUED BY:
DRAFTED BY: SL	CLIENT NAME: Anushka Gartaula Siwakoti			

This certificate confirms that the proposed development will meet the NSW government's requirements for sustainable building. It is issued in accordance with the commitments set out below. Terms used in this certificate, or in the commitments, have the meaning given by the document titled 'BASIX Definitions' (dated 10/09/2020) published by the Department. This document is available at www.planningportal.nsw.gov.au/definitions

Secretary
Date of issue: Friday, 12 June 2026
To be valid, this certificate must be submitted with a development application or lodged with a complying development certificate application within 3 months of the date of issue.



Project summary			
Project name	Lot 520 Gunyadu Street Austral		
Street address	GUNYADU STREET AUSTRAL 2179		
Local Government Area	Liverpool City Council		
Plan type and plan number	Deposited Plan dp1310900		
Section no.	-		
Project type	dwelling house (detached)		
No. of bedrooms	5		
Project score			
Water	✓ 40	Target	40
Thermal Performance (Do-it-yourself Method)	✓ Pass	Target	Pass
Energy	✓ 71	Target	70
Materials	✓ 41	Target	n/a
on Building Certificate			
RBC00045			
Certificate Prepared by:			
Name: Catherine M. RBC00045			
ABN (if applicable): 79638763150			

Paragon Building Certifiers Pty Ltd

RBC00045

Registered Certifier

APPROVED

Reference: 260513/01

Date: 11/09/2026

Description of project

Project address	
Project name	Lot 520 Gunyadu Street Austral
Street address	GUNYADU STREET AUSTRAL 2179
Local Government Area	Liverpool City Council
Plan type and plan number	Deposited Plan dp1310900
Lot no.	520
Section no.	-
Project type	
Project type	dwelling house (detached)
No. of bedrooms	5
Site details	
Site area (m ²)	361
Roof area (m ²)	162
Conditioned floor area (m ²)	172.0
Unconditioned floor area (m ²)	16.0
Total area of garden and lawn (m ²)	162
Roof area of the existing dwelling (m ²)	0

Assessor details and thermal loads			
NatHERS assessor number	n/a		
NatHERS certificate number	n/a		
Climate zone	n/a		
Area adjusted cooling load (MJ/m ² /year)	n/a		
Area adjusted heating load (MJ/m ² /year)	n/a		
Project score			
Water	✔ 40	Target	40
Thermal Performance (Do-it-Yourself Method)	✔ Pass	Target	Pass
Energy	✔ 71	Target	70
Materials	✔ -41	Target	n/a

Construction	Area - m ²	Additional insulation required	Options to address thermal bridging	Other specifications
external wall: framed (solid or reconstructed timber weatherboard); frame: timber - H2 treated softwood	22	3.00 (or 3.50 including construction) fibreglass batts or roll	nil	wall colour: Medium (solar absorptance 0.48-0.7)
internal wall shared with garage: plasterboard; frame: timber - H2 treated softwood	14.6	none	nil	
internal wall: plasterboard; frame: timber - H2 treated softwood	14.6	none	nil	
ceiling and roof: flat ceiling / flat roof: framed - metal roof: timber - H2 treated softwood	162	ceiling: 5 (up) roof: foil backed blanket; ceiling: foil backed blanket; roof: foil backed blanket	nil	roof colour: medium (solar absorptance 0.48-0.59); 0.5 to 1.0% of ceiling area uninsulated
Notes				
• Insulation specified in this Certificate must be installed in accordance with the ABCB Housing Provisions (Part 13.2.2) of the National Construction Code.				
• If the additional ceiling insulation listed in the table above is greater than R3.0, refer to the ABCB Housing Provisions (Part 13.2.3 (6)) of the National Construction Code.				
• In some climate zones, insulation should be installed with due consideration of condensation and associated interaction with adjoining building materials.				
• Thermal breaks must be installed in metal framed walls and applicable roofs in accordance with the ABCB Housing Provisions of the National Construction Code.				

Schedule of BASIX commitments

The commitments set out below regulate how the proposed development is to be carried out. It is a condition of any development consent granted, or complying development certificate issued, for the proposed development, that BASIX commitments be complied with.

Water Commitments	Show on DA plans	Show on CC/CDC plans & specs	Certifier check
Fixtures			
The applicant must install showerheads with a minimum rating of 5 star (> 4.5 but <= 6 L/min per spray force and/or coverage tests) in all showers in the development.		✓	✓
The applicant must install a toilet flushing system with a minimum rating of 4 star in each toilet in the development.		✓	✓
The applicant must install taps with a minimum rating of 4 star in the kitchen in the development.		✓	
The applicant must install basin taps with a minimum rating of 4 star in each bathroom in the development.		✓	
Alternative water			
Rainwater tank			
The applicant must install a rainwater tank of at least 1500 litres on the site. This rainwater tank must meet, and be installed in accordance with, the requirements of all applicable regulatory authorities.	✓	✓	✓
The applicant must configure the rainwater tank to collect rain runoff from at least 162 square metres of the roof area of the development (excluding the area of the roof which drains to any stormwater tank or private dam).		✓	✓
The applicant must connect the rainwater tank to:			
• the cold water tap that supplies each clothes washer in the development		✓	✓
• at least one outdoor tap in the development (Note: NSW Health does not recommend that rainwater be used for human consumption in areas with potable water supply.)		✓	✓

Thermal Performance and Materials commitments	Show on DA plans	Show on CC/CDC plans & specs	Certifier check
Ceiling fans			
The applicant must install at least one ceiling fan in at least one daytime habitable space, such as living room.	✓	✓	✓
• The minimum number and diameter of ceiling fans in a daytime habitable space must be installed in accordance with the ABCB Housing Provisions (Part 13.5.3) of the National Construction Code.	✓	✓	✓

Thermal Performance and Materials commitments	Show on DA plans	Show on CC/CDC plans & specs	Certifier check
Glazed windows, doors and skylights			
The applicant must install the windows, glazed doors and shading devices described in the table below, in accordance with the specifications listed in the table. Relevant overshadowing specifications must be satisfied for each glazed window and door.	✓	✓	✓
The dwelling may have 1 skylight (<0.7 square metres) which is not listed in the table.		✓	✓
The following requirements must also be satisfied in relation to each window and glazed door:	✓	✓	✓
• The applicant must install windows and glazed doors in accordance with the height and width, frame and glazing types listed in the table.	✓	✓	✓
• Each window and glazed door must have a U-value no greater than that listed and a Solar Heat Gain Coefficient (SHGC) within the range listed. Total system U-values and SHGC must be calculated in accordance with National Fenestration Rating Council (NFRC) conditions.	✓	✓	✓
The applicant must install the skylights described in the table below, in accordance with the specifications listed in the table. Total skylight area must not exceed 3 square metres (the 3 square metre limit does not include the optional additional skylight of less than 0.7 square metres that does not have to be listed in the table).	✓	✓	✓

Glazed window/door no.	Maximum height (mm)	Maximum width (mm)	Frame and glass specification	Shading device (Dimension within 10%)	Overshadowing
North facing					
FW5	1000.00	800.00	aluminium, single glazed (U-value: <=0.0, SHGC: 0.74 - 0.90)	eave 450 mm, 100 mm above head of window or glazed door	not overshadowed
FW6	1800.00	1250.00	aluminium, single glazed (U-value: <=0.0, SHGC: 0.74 - 0.90)	eave 450 mm, 100 mm above head of window or glazed door	not overshadowed
D5	2340.00	820.00	aluminium, single glazed (U-value: <=0.0, SHGC: 0.60 - 0.74)	overhang 600 mm, 320 mm above base of window or glazed door	not overshadowed
East facing					

Glazed window/door no.	Maximum height (mm)	Maximum width (mm)	Frame and glass specification	Shading device (Dimension within 10%)	Overshadowing
GW3	1500.00	1850.00	aluminium, single glazed (U-value: <=0.0, SHGC: 0.74 - 0.90)	eave 400 mm, 3500 mm above head of window or glazed door	not overshadowed
GW4	2000.00	1850.00	aluminium, single glazed (U-value: <=0.0, SHGC: 0.74 - 0.90)	eave 400 mm, 3500 mm above head of window or glazed door	not overshadowed
FW3	1500.00	1400.00	aluminium, single glazed (U-value: <=0.0, SHGC: 0.74 - 0.90)	eave 400 mm, 100 mm above head of window or glazed door	not overshadowed
FW4	1500.00	1400.00	aluminium, single glazed (U-value: <=0.0, SHGC: 0.74 - 0.90)	eave 400 mm, 100 mm above head of window or glazed door	not overshadowed
South facing					
GW1	1500.00	1850.00	aluminium, single glazed (U-value: <=0.0, SHGC: 0.74 - 0.90)	solid overhang 100 mm, 500 mm above head of window or glazed door	not overshadowed
GW2	1500.00	1850.00	aluminium, single glazed (U-value: <=0.0, SHGC: 0.74 - 0.90)	eave 400 mm, 3500 mm above head of window or glazed door	not overshadowed
FW1	1200.00	1850.00	aluminium, single glazed (U-value: <=0.0, SHGC: 0.74 - 0.90)	eave 1125 mm, 100 mm above head of window or glazed door	not overshadowed
FW2	1500.00	1400.00	aluminium, single glazed (U-value: <=0.0, SHGC: 0.74 - 0.90)	eave 400 mm, 100 mm above head of window or glazed door	not overshadowed
SD1	2300.00	2400.00	aluminium, single glazed (U-value: <=0.0, SHGC: 0.74 - 0.90)	eave 1125 mm, 100 mm above head of window or glazed door	not overshadowed
West facing					
GW5	1800.00	660.00	aluminium, single glazed (U-value: <=0.0, SHGC: 0.74 - 0.90)	eave 400 mm, 4880 mm above head of window or glazed door	not overshadowed

Glazed window/door no.	Maximum height (mm)	Maximum width (mm)	Frame and glass specification	Shading device (Dimension within 10%)	Overshadowing
GW6	1500.00	500.00	aluminium, single glazed (U-value: <=0.0, SHGC: 0.74 - 0.90)	eave 400 mm, 4035 mm above head of window or glazed door	not overshadowed
FW7	800.00	800.00	aluminium, single glazed (U-value: <=0.0, SHGC: 0.74 - 0.90)	eave 400 mm, 100 mm above head of window or glazed door	not overshadowed

Energy Commitments	Show on DA plans	Show on CC/CDC plans & specs	Certifier check
Hot water			
The applicant must install the following hot water system in the development, or a system with a higher energy rating: gas instantaneous with a performance of 5 stars.	✓	✓	✓
Cooling system			
The applicant must install the following cooling system, or a system with a higher energy rating, in at least 1 living area: 3-phase air conditioning. Energy rating EER 3.0 - 3.5		✓	✓
The applicant must install the following cooling system, or a system with a higher energy rating, in at least 1 bedroom: 3-phase air conditioning. Energy rating EER 3.0 - 3.5		✓	✓
Heating system			
The applicant must install the following heating system, or a system with a higher energy rating, in at least 1 living area: 3-phase air conditioning. Energy rating EER 3.0 - 3.5		✓	✓
The applicant must install the following heating system, or a system with a higher energy rating, in at least 1 bedroom: 3-phase air conditioning. Energy rating EER 3.0 - 3.5		✓	✓
Ventilation			
The applicant must install the following exhaust systems in the development:			
At least 1 Bathroom: no mechanical ventilation (ie. natural). Operation control: n/a		✓	✓
Kitchen: individual fan, ducted to facade. Operation control: manual switch on/off		✓	✓
Laundry: natural ventilation only, or no laundry. Operation control: n/a		✓	✓
Artificial lighting			
The applicant must ensure that a minimum of 60% of light fixtures are fitted with fluorescent, compact fluorescent, or light-emitting diode (LED) lamps.		✓	✓
Natural lighting			
The applicant must install a window and/or skylight in 3 bathroom(s)/toilet(s) in the development for natural lighting.	✓	✓	✓

Energy Commitments	Show on DA plans	Show on CC/CDC plans & specs	Certifier check
Other			
The applicant must install a gas cooktop & electric oven in the kitchen of the dwelling.		✓	
The applicant must install a fixed outdoor clothes drying line as part of the development.		✓	

Legend
In these commitments, "applicant" means the person carrying out the development.
Commitments identified with a ✓ in the "Show on DA plans" column must be shown on the plans accompanying the development application for the proposed development (if a development application is to be lodged for the proposed development).
Commitments identified with a ✓ in the "Show on CC/CDC plans and specs" column must be shown in the plans and specifications accompanying the application for a construction certificate / complying development certificate for the proposed development.
Commitments identified with a ✓ in the "Certifier check" column must be certified by a certifying authority as having been fulfilled, before a final occupation certificate (either interim or final) for the development may be issued.


REV	DATE	DESCRIPTION	BY
4	7-07-2026	Site Address updated	
3	23-06-2026	DA ISSUE	



RUBY HOMES


THIS DRAWING IS THE EXCLUSIVE PROPERTY OF THE DEVELOPER & THE REPRODUCTION OF ANY PART WITHOUT THE PRIOR WRITTEN CONSENT OF THE DEVELOPER IS A VIOLATION OF APPLICABLE LAWS. IN NO EVENT SHALL THE DEVELOPER BE HELD LIABLE FOR SPECIAL COLLATERAL, INCIDENTAL OR CONSEQUENTIAL LIABILITY IN CONNECTION WITH THE USE OF THIS DIGITAL DATA ONCE RELEASED FROM THE DEVELOPER'S OFFICE. THIS DRAWING IS TO BE READ & UNDERSTOOD IN CONJUNCTION WITH THE STRUCTURAL, MECHANICAL, ELECTRICAL & / OR ANY OTHER CONSULTANT'S DOCUMENTATION AS MAY BE APPLICABLE TO THE PROJECT PRIOR TO THE START OF ANY WORKS AND FOR ITS DURATION.

PROJECT:	DRAWING TITLE:	NORTH:	LOT NO:	DATE:	SCALE:	DRAWING No:	REV:
46 Gunyadu Street	BASIX		520	7-09-2026		CC.16	4
Lot 520 in Dp 1310900 at 46 Gunyadu Street Austral NSW 2179			DRAWN BY: AS	CHECKED BY: RH			ISSUED BY:
			DRAFTED BY: SL	CLIENT NAME: Anushka Gartaula Siwakoti			

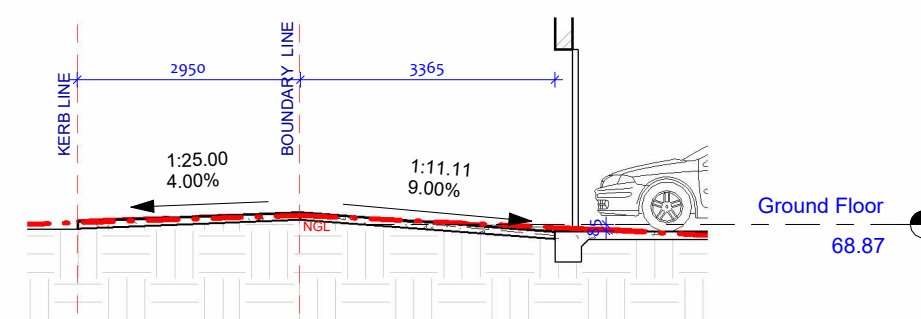


1 DRIVEWAY SECTION
1 : 100

4	7-07-2026	Site Address updated	
3	23-06-2026	DA ISSUE	
REV	DATE	DESCRIPTION	BY

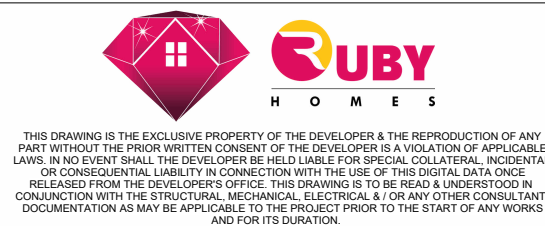

PROJECT:
46 Gunyadu Street
Lot 520 in Dp 1310900 at 46
Gunyadu Street Austral NSW 2179

DRAWING TITLE:
DRIVEWAY PLAN

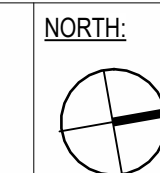

LOT NO: 520	DATE: 7-09-2026	SCALE: 1 : 100	DRAWING No:	REV: 4
DRAWN BY: AS	CHECKED BY: RH		CC.18	ISSUED BY:
DRAFTED BY: SL	CLIENT NAME: Anushka Gartaula Siwakoti			

ABCB HOUSING PROVISIONS : PART 10.2 WET AREA WATERPROOFING

10.2.1 Wet Areas

1.

Building elements in wet areas within a building must be protected with a waterproofing system.
2.

The waterproofing system in (1) must be either waterproof or water resistant in accordance with 10.2.2 to 10.2.6.

10.2.2 Shower Area (enclosed and unenclosed)

1.

For a shower area with a hob, step-down or level threshold, the following applies:

a.

The floor of the shower area must be waterproof, including any hob or step-down (see Figure 10.2.2); and

b.

The walls of the shower area must be waterproof not less than 1800 mm above the floor substrate (see Figure 10.2.2).

c.

Wall junctions and joints within the shower area must be waterproof not less than 40 mm either side of the junction (see Figure 10.2.2).

d.

Wall/floor junctions within the shower area must be waterproof (see Figure 10.2.2).

e.

Penetrations within the shower area must be waterproof.

2.

A shower with a preformed shower base must also comply with the requirements of (1), except for (a) which is not applicable.
- Figure 10.2.2: Extent of treatment for shower areas - concrete compressed fibre-cement and fibre-cement sheet floors.
-
- Figure Notes
Wall/floor junction heights are to be as per 10.2.2 to 10.2.6 (as applicable).
- Notes
Where a shower is above a bath or spa, use requirements for shower.
- 10.2.3 Area outside shower area
1.

For concrete, compressed fibre-cement and fibre-cement sheet flooring, the floor of the room must be water resistant.

2.

For timber floors including particleboard, plywood and other timber based flooring materials, the floor of the room must be waterproof.

3.

Wall/floor junctions must be -

a.

waterproof, and

b.

where a flashing is used, the horizontal leg must be not less than 40 mm.
- 10.2.4 Areas adjacent to baths and spas without showers
1.

For areas adjacent to all baths and spas, the following applies:

a.

For concrete, compressed fibre-cement and fibre-cement sheet flooring, the floor of the room must be water resistant.

b.

For timber floors including particleboard, plywood and other timber based flooring materials, the floor of the room must be waterproof.

c.

Tap and spout penetrations must be waterproof where they occur in horizontal surfaces.

2.

For areas adjacent to non-freestanding baths and spas, the following applies:

a.

Walls must be water resistant (see Figure 10.2.4a and Figure 10.2.4b):
 - to a height of not less than 150mm above the vessel, for the extent of the vessel, where the vessel is within 75mm of a wall; and
 - for all exposed surfaces below vessel lip.

b.

Wall junctions and joints must be water resistant within 150mm above a vessel for the extent of the vessel.

c.

Wall/floor junctions must be waterproof for the extent of the vessel (see Figure 10.2.4a and Figure 10.2.4b).

3.

For inserted baths and spas, the following applies:

a.

For floors and horizontal surfaces:
 - Any shelf area adjoining the bath or spa must be waterproof and include a waterstop under the vessel lip.
 - There are no requirements for the floor under a bath or spa.

b.

For walls:
 - Waterproof to not less than 150mm above the lip of a bath or spa.
 - There are no requirements for the floor under a bath or spa.

c.

For wall junctions and joints, the following applies:
 - Waterproof junctions within 150mm of a bath or spa.
 - There are no requirements for junctions and joints in walls beneath the lip of a bath or spa.

d.

Tap and spout penetrations must be waterproof where they occur in horizontal surfaces.

Figure 10.2.4a: Areas adjacent to baths and spas without showers for concrete, compressed fibre-cement and fibre-cement sheet flooring

Figure 10.2.4b: Areas adjacent to baths and spas without showers for timber floors including particle-board, plywood and other floor materials

10.2.5 Other areas

1.

For walls adjoining other types of vessels (e.g. sink, basin or laundry tub), the following applies:

a.

Walls must be water resistant to a height of not less than 150mm above the vessel, for the extent of the vessel, where the vessel is within 75 mm of a wall (see Figure 10.2.5.)

b.

Waterproof wall junctions where a vessel is fixed to a wall.

c.

Waterproof tap and spout penetrations where they occur in surfaces required to be waterproof or water resistant.

2.

For laundries and WCs, the following applies:

a.

The floor of the room must be water resistant.

b.

Wall/floor junctions must be water resistant, and where a flashing is used, the horizontal leg must not be less than 40 mm.

3.

For WCs with handheld bidet spray installations, the following applies:

a.

The floor of the room must be waterproof.

b.

Walls must be -
 - waterproof in WC area within a 900 mm radius from the wall connection of the handheld bidet spray device to a height of not less than 150mm above the floor substrate; and
 - water resistant in WC area within a 900 mm radius from the wall connection of the handheld bidet device to not less than 1200 mm above the finished floor level of the WC.

c.

Wall junctions within the WC area within 900 mm radius from the wall connection of the handheld bidet spray device must be waterproof.

d.

Wall/floor junctions within the WC area within 1000 mm radius from the wall connection of the handheld bidet spray device must be waterproof.

e.

Penetrations in the WC area must be waterproof.

Figure 10.2.5: Bath and vessel abutting wall - areas to be protected

10.2.6 Waterproofing systems

1.

For the purposes of this Part, a waterproofing system is deemed -

a.

waterproof, if it complies with (2); or

b.

water resistant, if it complies with (3).

2.

For a waterproofing system required to be waterproof in accordance with 10.2.2 to 10.2.5, the materials nominated in 10.2.8 must be used.

3.

For a waterproofing system required to be water resistant in accordance with 10.2.2 to 10.2.5, the materials nominated in 10.2.9 must be used in conjunction with the materials in 10.2.10.

10.2.12 Construction of wet area floors - falls

Where a floor waste is installed -

a.

the minimum continuous fall of a floor plane to the waste must be 1:80; and

b.

the maximum continuous fall of a floor plane to the waste must be 1:50.

4	7-07-2026	Site Address updated	
3	23-06-2026	DA ISSUE	
REV	DATE	DESCRIPTION	BY




RUBY HOMES

THIS DRAWING IS THE EXCLUSIVE PROPERTY OF THE DEVELOPER & THE REPRODUCTION OF ANY PART WITHOUT THE PRIOR WRITTEN CONSENT OF THE DEVELOPER IS A VIOLATION OF APPLICABLE LAWS. IN NO EVENT SHALL THE DEVELOPER BE HELD LIABLE FOR SPECIAL COLLATERAL, INCIDENTAL OR CONSEQUENTIAL LIABILITY IN CONNECTION WITH THE USE OF THIS DIGITAL DATA ONCE RELEASED FROM THE DEVELOPER'S OFFICE. THIS DRAWING IS TO BE READ & UNDERSTOOD IN CONJUNCTION WITH THE STRUCTURAL, MECHANICAL, ELECTRICAL & / OR ANY OTHER CONSULTANT'S DOCUMENTATION AS MAY BE APPLICABLE TO THE PROJECT PRIOR TO THE START OF ANY WORKS AND FOR ITS DURATION.

PROJECT:
46 Gunyadu Street

Lot 520 in Dp 1310900 at 46 Gunyadu Street Austral NSW 2179

DRAWING TITLE:
WATERPROOFING DETAILS

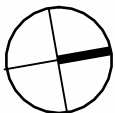NORTH:


LOT NO:	DATE:	SCALE:	DRAWING No:	REV:
520	7-09-2026	1 : 50	CC.19	4
DRAWN BY:	CHECKED BY:			ISSUED BY:
AS	RH			
DRAFTED BY:	CLIENT NAME:			
SL	Anushka Gartaula Siwakoti			

CC ISSUE

A3

BUILDING SPECIFICATIONS

National Construction Code – Volume 2, Amendment 1 – Building Code of Australia 2022 & Housing Provisions Standard 2022

SITE PREPARATION

- PART 3.1 OF THE NCC VOLUME 2, AMENDMENT 1 - BUILDING CODE OF AUSTRALIA 2022 & HOUSING PROVISIONS STANDARD 2022.

EARTHWORKS

- TO BE CARRIED OUT IN ACCORDANCE WITH THE REQUIREMENTS OF THE ENVIRONMENTAL PLANNING & ASSESSMENT ACT 1979 AND DEVELOPMENT CONSENT CONDITIONS
- PART 3.2 OF THE NCC VOLUME 2, AMENDMENT 1 - BUILDING CODE OF AUSTRALIA 2022 & HOUSING PROVISIONS STANDARD 2022.
- AS 4678:2002 - EARTH-RETAINING STRUCTURES

DRAINAGE

- PART 3.3 OF THE NCC VOLUME 2, AMENDMENT 1 - BUILDING CODE OF AUSTRALIA 2022 & HOUSING PROVISIONS STANDARD 2022.
- AS/NZS 3500.1:2021 - PLUMBING & DRAINAGE - WATER SERVICES
- AS/NZS 3500.2:2021 - PLUMBING & DRAINAGE - SANITARY PLUMBING & DRAINAGE
- AS/NZS 3500.3:2021 - PLUMBING & DRAINAGE - STORMWATER DRAINAGE
- AS/NZS 3500.4:2021 - PLUMBING & DRAINAGE - HEATED WATER SERVICES

STRUCTURAL WORK

- Part 2.2 OF THE NCC VOLUME 2, AMENDMENT 1 - BUILDING CODE OF AUSTRALIA 2022 & HOUSING PROVISIONS STANDARD 2022.
- AS 4100:2020– STEEL STRUCTURES CODES
- AS/NZS 1170.0:2002 – GENERAL PRINCIPLES
- AS/NZS 1170.1:2002 – PARTS 1 PERMANENT, IMPOSED AND OTHER ACTIONS
- AS/NZS 1170.2:2021 – PART 2 WIND ACTIONS
- AS 3700:2018– SAA MASONRY CODE
- AS 1684.3:2021- RESIDENTIAL TIMBER FRAMED CONSTRUCTION

FOOTINGS & SLABS

- PART 4 OF THE NCC VOLUME 2, AMENDMENT 1 - BUILDING CODE OF AUSTRALIA 2022 & HOUSING PROVISIONS STANDARD 2022.
- AS 2159:2009 - PILING - DESIGN & INSTALLATION
- AS 2870:2011 - RESIDENTIAL SLABS & FOOTINGS
- AS 3600:2018 - CONCRETE STRUCTURES

MASONRY

- PART 5 OF THE NCC VOLUME 2, AMENDMENT 1 - BUILDING CODE OF AUSTRALIA 2022 & HOUSING PROVISIONS STANDARD 2022.
- AS 3700:2018 - MASONRY STRUCTURES

FRAMING

- PART 6 OF THE NCC VOLUME 2, AMENDMENT 1 - BUILDING CODE OF AUSTRALIA 2022 & HOUSING PROVISIONS STANDARD 2022.
- AS 1684.2:2021 - RESIDENTIAL TIMBER-FRAMED CONSTRUCTION - NON- CYCLONIC AREAS
- AS 1720.1:2010 - TIMBER STRUCTURES - DESIGN METHODS
- AS 4100:2020 - STEEL STRUCTURES
- AS 3660.1:2014 – TERMITE MANAGEMENT SYSTEM

ROOF & WALL CLADDING

- PART 7 OF THE NCC VOLUME 2, AMENDMENT 1 - BUILDING CODE OF AUSTRALIA 2022 & HOUSING PROVISIONS STANDARD 2022.
- AS 1273:1991 - UNPLASTICIZED PVC (UPVC) DOWNPIPES & FITTINGS FOR RAINWATER
- AS 1562.1:2018 - DESIGN & INSTALLATION OF SHEET ROOF & WALL CLADDING - METAL
- AS/NZS 1562.3:2006 - DESIGN & INSTALLATION OF SHEET ROOF & WALL CLADDING - PLASTIC
- AS 2049:2002 - ROOF TILES
- AS 2050:2018 - INSTALLATION OF ROOF TILES
- AS 4285:2019 – ROOFLIGHTS

GLAZING

- PART 8 OF THE NCC VOLUME 2, AMENDMENT 1 - BUILDING CODE OF AUSTRALIA 2022 & HOUSING PROVISIONS STANDARD 2022.
- AS 1288:2021 - GLASS IN BUILDINGS - SELECTION & INSTALLATION
- AS 2047:2014 - WINDOWS & EXTERNAL GLAZED DOORS IN BUILDINGS
- AS/NZS 2208:1996 - SAFETY GLAZING MATERIALS IN BUILDINGS

FIRE SAFETY

- PART 9 OF THE NCC VOLUME 2, AMENDMENT 1 - BUILDING CODE OF AUSTRALIA 2022 & HOUSING PROVISIONS STANDARD 2022.
- AS 3786:2014 - SMOKE ALARMS USING SCATTERED LIGHT, TRANSMITTED LIGHT OR IONIZATION

HEALTH & AMENITY

- PART 10 OF THE NCC VOLUME 2, AMENDMENT 1 - BUILDING CODE OF AUSTRALIA 2022 & HOUSING PROVISIONS STANDARD 2022.
- AS/NZS ISO 717.1:2004 - ACOUSTICS - RATING OF SOUND INSULATION IN BUILDINGS & OF BUILDING ELEMENTS - AIRBORNE SOUND INSULATION
- AS ISO 717.2:2004 - ACOUSTICS - RATING OF SOUND INSULATION IN BUILDINGS & OF BUILDING ELEMENTS - IMPACT SOUND INSULATION
- AS 1668.2:2012 - THE USE OF VENTILATION & AIR CONDITIONING IN BUILDINGS - MECHANICAL VENTILATION IN BUILDINGS
- AS 1668.4:2012 - THE USE OF VENTILATION & AIR CONDITIONING IN BUILDINGS - NATURAL VENTILATION OF BUILDINGS
- AS/NZS 1680.0:2009 - INTERIOR LIGHTING - SAFE MOVEMENT
- AS 3740:2021 - WATERPROOFING OF DOMESTIC WET AREAS
- AS 3000:2018 – ELECTRICAL INSTALLATION
- BCA Part 10.8.1, AS4200.1 & AS4200.2 – PLIABLE BUILDING MEMBRANE INSTALLED.

WATERPROOFING

- PART 10.2 OF THE NCC VOLUME 2, AMENDMENT 1 - BUILDING CODE OF AUSTRALIA 2022 & HOUSING PROVISIONS STANDARD 2022
- AS 3740:2021– WATERPROOFING TO WET AREA
- AS 4654:2012 – EXTERNAL WET AREAS

SAFE MOVEMENT & ACCESS

- PART 11 OF THE NCC VOLUME 2, AMENDMENT 1 - BUILDING CODE OF AUSTRALIA 2022 & HOUSING PROVISIONS STANDARD 2022.
- AS 1428.1:2009 - DESIGN FOR ACCESS & MOBILITY – GENERAL REQUIREMENTS FOR ACCESS - NEW BUILDING WORK
- AS 1657:2018 - FIXED PLATFORMS, WALKWAYS, STAIRWAYS & LADDERS - DESIGN, CONSTRUCTION & INSTALLATION

HANDRAILS & BALUSTRADE

- PART 11.3.3 OF THE NCC VOLUME 2, AMENDMENT 1 - BUILDING CODE OF AUSTRALIA 2022 & HOUSING PROVISIONS STANDARD 2022.
- PART 11.3.4 OF THE NCC VOLUME 2, AMENDMENT 1 - BUILDING CODE OF AUSTRALIA 2022 & HOUSING PROVISIONS STANDARD 2022.
- PART 11.3.5 OF THE NCC VOLUME 2, AMENDMENT 1 - BUILDING CODE OF AUSTRALIA 2022 & HOUSING PROVISIONS STANDARD 2022.
- AS 1170.1:2002 – BALUSTRADE INSTALLATION

PROTECTION OF OPENABLE WINDOW

PART 11.3.7 AND 11.3.8 OF THE NCC VOLUME 2, AMENDMENT 1 - BUILDING CODE OF AUSTRALIA 2022 & HOUSING PROVISIONS STANDARD 2022.

ENERGY EFFICIENCY

- PART 13 OF THE NCC VOLUME 2, AMENDMENT 1 - BUILDING CODE OF AUSTRALIA 2022 & HOUSING PROVISIONS STANDARD 2022 & BASIX CERTIFICATE.

HEATING APPLIANCES, FIREPLACES, CHIMNEYS AND FLUES

- PART 12.4 OF THE NCC VOLUME 2, AMENDMENT 1 - BUILDING CODE OF AUSTRALIA 2022 & HOUSING PROVISIONS STANDARD 2022.

MECHANICAL VENTILATION

- EXHAUST FROM A BATHROOM, SANITARY COMPARTMENT TO DISCHARGE DIRECTLY TO OUTDOOR AIR WITH MINIMUM FLOW RATE OF 25L/S & MAKE-UP AIR VIA OPENINGS TO AN ADJACENT ROOM WITH A FREE AREA OF 14,000 MM². THIS EXHAUST SYSTEM MUST BE INTERLOCKED WITH LIGHT SWITCH AND INCLUDE RUN-ON TIMER SO THAT THE EXHAUST SYSTEM CONTINUES TO OPERATE FOR 10 MINUTES AFTER THE LIGHT SWITCH IS OFF.
- ANY INSTALLED - KITCHEN RANGEHOOD EXHAUST TO DISCHARGE DIRECTLY OR VIA DUCT TO OUTDOOR AIR WITH MINIMUM FLOW RATE OF 40L/S & MAKE-UP AIR VIA OPENINGS TO AN ADJACENT ROOM WITH A FREE AREA OF 14,000 MM².
- LAUNDRY EXHAUST TO DISCHARGE DIRECTLY OR VIA DUCT TO OUTDOOR AIR WITH MINIMUM FLOW RATE OF 40L/S & MAKE-UP AIR VIA OPENINGS TO AN ADJACENT ROOM WITH A FREE AREA OF 14,000 MM².



TERMITE SHEET

- TERMITE SHEET EXTENDS THROUGH THE ENTIRE MASONRY LEAF AND IS VISIBLE AT THE FINISHED FACE OF THE WALL.

OVERFLOW TO BALCONY:

- SURFACE DRAIN & OVERFLOW TO BALCONY


RBC00045

Registered Certifier

APPROVED

Reference: 260513/01



Date: 11/09/2026

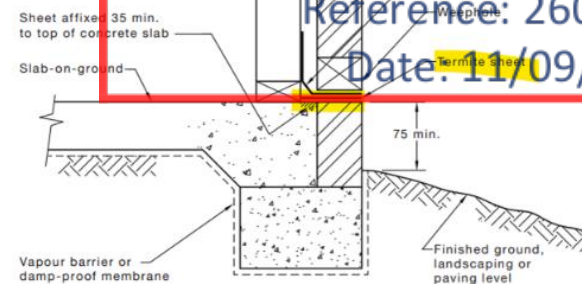

(a) Masonry veneer with separate strip footings

DIMENSIONS IN MILLIMETRES


FIGURE 5.5 (in part) TYPICAL SHEET INSTALLATION TO EXTERNAL WALL WITH CONCRETE FLOOR SLAB

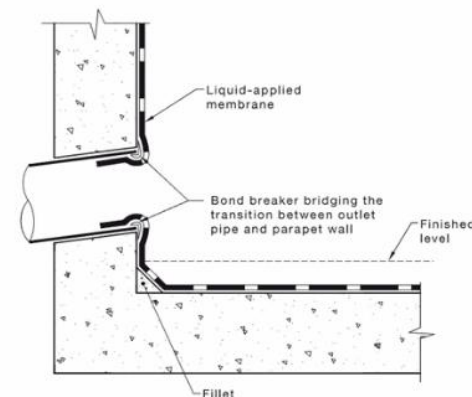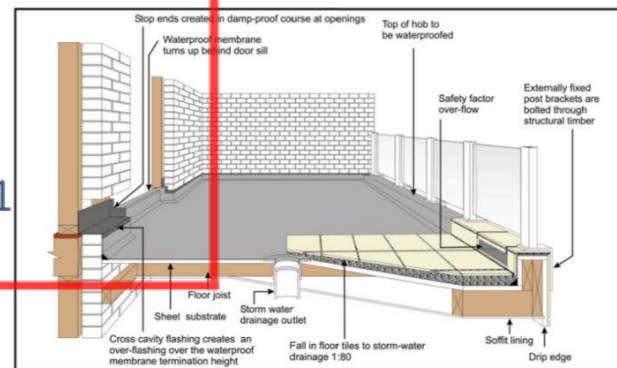

(a) Overflow through parapet

DPC FOR BRICKS

DAMP-PROOF COURSE (DPC) TO EXTENDS THROUGH THE ENTIRE MASONRY LEAF AND NEED TO BE VISIBLE AT THE FINISHED FACE OF THE WALL FROM OUTSIDE

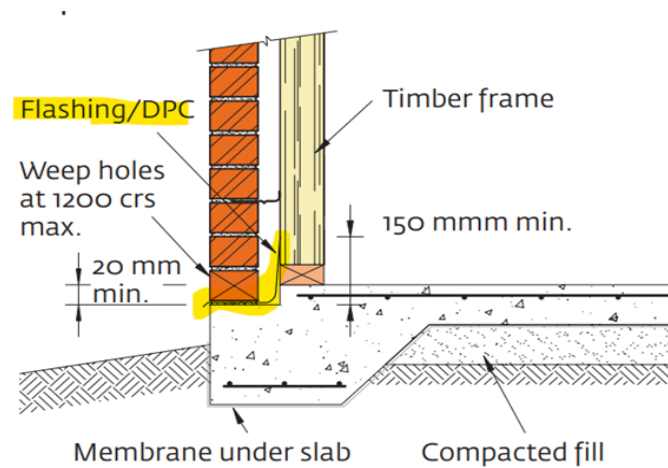

WATERPROOFING

FALL TO FLOOR WASTE TO BE MINIMUM 1:80 TO MAXIMUM 1:50

Figure 10.2.29: Typical membrane termination at drainage outlet



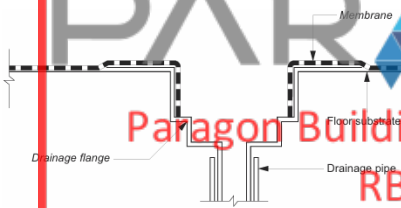


Figure 10.2.24: Typical bathroom door details for whole bathroom waterproofing

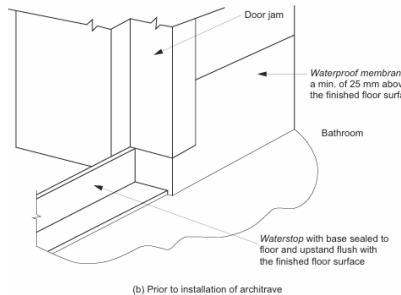


BASIN & BATHTUB:

Figure 10.2.5: Bath and vessel abutting wall — areas to be protected

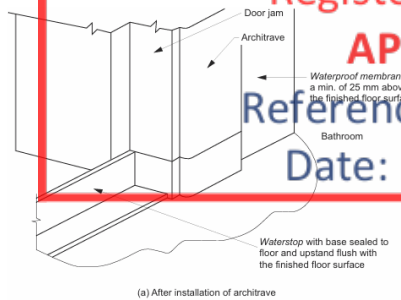


(a) Vessel abutting wall

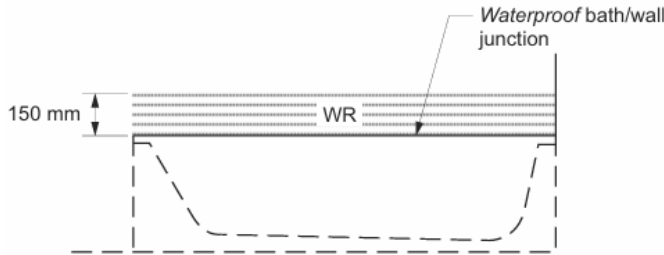


(b) Wall/bath junction

ENCLOSED SHOWER AREA

Figure 10.2.17: Typical hobless construction

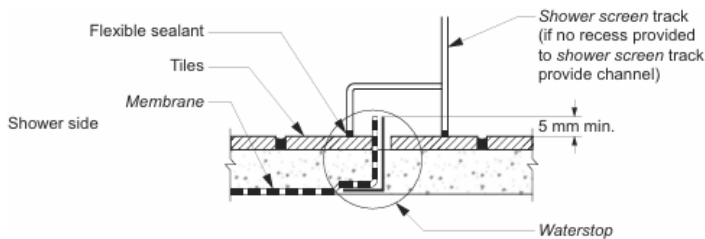

Extent of treatment for shower areas — concrete compressed fibre-cement and fibre-cement sheet floors

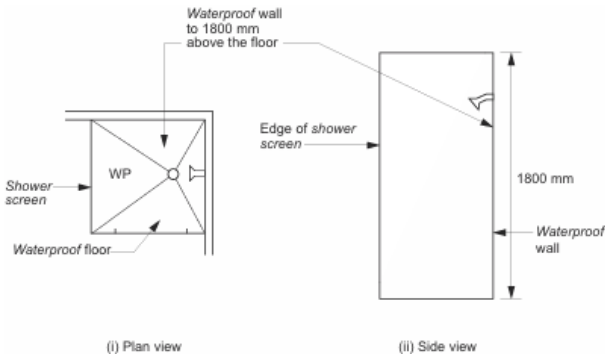

(a) Enclosed shower