

FOR CONSTRUCTION

LOT 349 - 4 BANTAM STREET AUSTRAL. IN DP 1294400.
PROPOSED CONSTRUCTION OF A TWO STOREY DWELLING



OnSite Certification Ltd
Reference: 260048
Date: 14/09/2026
Andrew Schuman
Director/ Principal Certifier
BDC2940
Consultant to be prepared and document remains responsible for accuracy

BASIX COMMITMENTS		Certificate number: 18648255_02 Date of issue: Wednesday, 09 September 2026
WATER		
LANDSCAPE	103m2	
TOILETS	4 STARS	
KITCHEN TAPS	4 STARS	
SHOWER HEADS	5 STAR (>4.5 but <=6 Umin)	
BASIN TAPS	4 STARS	
ALTERNATIVE WATER	1500L RAINWATER TANK	
ROOF WATER TO TANK	165m2	
ALT.WATER USES- TANK	LAUNDRY	
ALT. WATER USES - RETIC	ALL TOILETS + ONE OUTDOOR TAP	
OUTDOOR SPA	NA	
ENERGY		
HOT WATER	GAS INSTANTANEOUS - 5 STAR	
AIR-CON (HEATING)	3 PHASE DUCTED - EER 3.0-3.5	
AIR-CON (COOLING)	3 PHASE DUCTED - EER 3.0-3.5	
VENTILATION - BATHROOM	NONE/ NATURAL VENTILATION	
VENTILATION - KITCHEN	DUCTED - MANUAL SWITCH	
VENTILATION - LAUNDRY	NONE/ NATURAL VENTILATION	
PV SYSTEM	NA	
COOKTOP	GAS	
OVEN	ELECTRIC	
CLOTHES DRYING	OUTDOOR CLOTHESLINE	
LIGHTING	DEDICATED LED	

AC	AIR CONDITIONING UNIT
AD	ALUMINUM DOOR WINDOW
BA	BATHSHADE TYPE
BG	BOX GUTTER
BR1, BR2, etc	BRICK FACE TYPE
CAP	METAL CAPPING
CND	CONCRETE FLOOR
CPT	CARPET
CRT	CONCRETE ROOF TILES
CR1, CR2, etc.	CEMENT RENDER TYPE/ COLOUR
DP/S	DOWN PIPE
DW	DISH WASHER
ED	ENTRY DOOR
F	FRIDGE
FAS	FASCIA
FET	FEATURE TILE
FT, FT1, FT2, etc	FLOOR TILES
FW	FLOOR WASTE
GD	GARAGE DOOR
GUT	GUTTER
HWU	HOT WATER UNIT
HYB	HYBRID FLOOR
L	LINEN
MR	METAL ROOF
MW	MICROWAVE OVEN
NGL	NATURAL GROUND LEVEL
OBS	OBSCURED GLASS
P	PANTRY
R	ROBE
RL	REDUCED LEVEL
RWH	RAIN WATER HEAD
RWT	RAIN WATER TANK
S	STORAGE
TOW	TOP OF WALL
TL	TIMBER LAMINATE
WC	WATER CLOSET
WM	WASHING MACHINE
SD	SMOKE DETECTOR

Sheet List				
Sheet No.	Sheet Name	Drawn By	Current Revision Date	Current Revision Issued To
CDC.01	COVER SHEET	AS	10-07-2026	CDC ISSUE
CDC.02A	GENERAL NOTES	AS	01-07-2026	CDC ISSUE
CDC.02B	GENERAL NOTES	AS	01-07-2026	CDC ISSUE
CDC.03	LOCATION PLAN AND SITE PLAN	AS	10-07-2026	CDC ISSUE
CDC.04	SITE ANALYSIS AND SEDIMENT CONTROL	AS	01-07-2026	CDC ISSUE
CDC.05	GROUND FLOOR PLAN	AS	01-07-2026	CDC ISSUE
CDC.06	FIRST FLOOR LEVEL	AS	01-07-2026	CDC ISSUE
CDC.07	ROOF PLAN	AS	01-07-2026	CDC ISSUE

Sheet List				
Sheet No.	Sheet Name	Drawn By	Current Revision Date	Current Revision Issued To
CDC.08	ELEVATION 01	AS	01-07-2026	CDC ISSUE
CDC.09	ELEVATION 02	AS	01-07-2026	CDC ISSUE
CDC.10	SECTIONS	AS	01-07-2026	CDC ISSUE
CDC.11	FLOOR AREA PLAN	AS	01-07-2026	CDC ISSUE
CDC.12	RENTABLE AREA PLAN	AS	01-07-2026	CDC ISSUE
CDC.14	COLOR SCHEDULE	AS	01-07-2026	CDC ISSUE
CDC.15	LANDSCAPE PLAN	AS	01-07-2026	CDC ISSUE
CDC.16	WATERPROOFING DETAILS	AS	01-07-2026	CDC ISSUE

NOTE: ALL IMAGES ARE FOR ILLUSTRATION ONLY AND ARE SUBJECT TO VARIATION AND TO AVAILABILITY OF MATERIALS.

1110-07-2026Building shifted by 270mm rear to comply with articulation

901-07-2026CDC ISSUE

826-06-2026Bed3 Removed and area adjusted to 270 Sq.m - Ekta

REVDATEDESCRIPTIONBY

THIS DRAWING IS THE EXCLUSIVE PROPERTY OF THE DEVELOPER & THE REPRODUCTION OF ANY PART WITHOUT THE PRIOR WRITTEN CONSENT OF THE DEVELOPER IS A VIOLATION OF APPLICABLE LAWS. IN NO EVENT SHALL THE DEVELOPER BE HELD LIABLE FOR SPECIAL, COLLATERAL, INCIDENTAL OR CONSEQUENTIAL LIABILITY IN CONNECTION WITH THE USE OF THIS DIGITAL DATA ONCE RELEASED FROM THE DEVELOPERS OFFICE. THIS DRAWING IS TO BE READ & UNDERSTOOD IN CONJUNCTION WITH THE STRUCTURAL, MECHANICAL, ELECTRICAL & / OR ANY OTHER CONSULTANTS DOCUMENTATION AS MAY BE APPLICABLE TO THE PROJECT PRIOR TO THE START OF ANY WORKS AND FOR ITS DURATION.

PROJECT:
4 BANTAM STREET

DRAWING TITLE:
COVER SHEET

NORTH:

LOT 349 4 BANTAM STREET
AUSTRAL 2179

LOT NO:
349

DRAWN BY:
AS

DRAFTED BY:
ID

DATE:
9-09-2026

CHECKED BY:
RH

CLIENT NAME:
Md Reza Razaak Khan & Nusrat Afia Neshat

SCALE:
As indicated

DRAWING No:
CDC.01

REV:
11

ISSUED BY:

BUILDING SPECIFICATIONS

National Construction Code – Volume 2, Amendment 1 – Building Code of Australia 2022 & Housing Provisions Standard 2022

SITE PREPARATION

- PART 3.1 OF THE NCC VOLUME 2, AMENDMENT 1 - BUILDING CODE OF AUSTRALIA 2022 & HOUSING PROVISIONS STANDARD 2022.

EARTHWORKS

- TO BE CARRIED OUT IN ACCORDANCE WITH THE REQUIREMENTS OF THE ENVIRONMENTAL PLANNING & ASSESSMENT ACT 1979 AND DEVELOPMENT CONSENT CONDITIONS
- PART 3.2 OF THE NCC VOLUME 2, AMENDMENT 1 - BUILDING CODE OF AUSTRALIA 2022 & HOUSING PROVISIONS STANDARD 2022.
- AS 4678:2002 - EARTH-RETAINING STRUCTURES

DRAINAGE

- PART 3.3 OF THE NCC VOLUME 2, AMENDMENT 1 - BUILDING CODE OF AUSTRALIA 2022 & HOUSING PROVISIONS STANDARD 2022.
- AS/NZS 3500.1:2021 - PLUMBING & DRAINAGE - WATER SERVICES
- AS/NZS 3500.2:2021 - PLUMBING & DRAINAGE - SANITARY PLUMBING & DRAINAGE
- AS/NZS 3500.3:2021 - PLUMBING & DRAINAGE STORMWATER DRAINAGE
- AS/NZS 3500.4:2021 - PLUMBING & DRAINAGE - HEATED WATER SERVICES

STRUCTURAL WORK

- Part 2.2 OF THE NCC VOLUME 2, AMENDMENT 1 - BUILDING CODE OF AUSTRALIA 2022 & HOUSING PROVISIONS STANDARD 2022.
- AS 4100:2020 - STEEL STRUCTURES CODES
- AS/NZS 1170.0:2002 - GENERAL PRINCIPLES
- AS/NZS 1170.1:2002 - PARTS 1 PERMANENT, IMPOSED AND OTHER ACTIONS
- AS/NZS 1170.2:2021 - PART 2 WIND ACTIONS
- AS 3700:2018 - SAA MASONRY CODE
- AS 1684.3:2021 - RESIDENTIAL TIMBER FRAMED CONSTRUCTION

FOOTINGS & SLABS

- PART 4 OF THE NCC VOLUME 2, AMENDMENT 1 - BUILDING CODE OF AUSTRALIA 2022 & HOUSING PROVISIONS STANDARD 2022.
- AS 2159:2009 - PILING - DESIGN & INSTALLATION
- AS 2870:2011 - RESIDENTIAL SLABS & FOOTINGS
- AS 3600:2018 - CONCRETE STRUCTURES

MASONRY

- PART 5 OF THE NCC VOLUME 2, AMENDMENT 1 - BUILDING CODE OF AUSTRALIA 2022 & HOUSING PROVISIONS STANDARD 2022.
- AS 3700:2018 - MASONRY STRUCTURES

FRAMING

- PART 6 OF THE NCC VOLUME 2, AMENDMENT 1 - BUILDING CODE OF AUSTRALIA 2022 & HOUSING PROVISIONS STANDARD 2022.
- AS 1684.2:2021 - RESIDENTIAL TIMBER-FRAMED CONSTRUCTION - NON- CYCLONIC AREAS
- AS 1720.1:2010 - TIMBER STRUCTURES - DESIGN METHODS
- AS 4100:2020 - STEEL STRUCTURES
- AS 3660.1:2014 - TERMITE MANAGEMENT SYSTEM

ROOF & WALL CLADDING

- PART 7 OF THE NCC VOLUME 2, AMENDMENT 1 - BUILDING CODE OF AUSTRALIA 2022 & HOUSING PROVISIONS STANDARD 2022.
- AS 1273:1991 - UNPLASTICIZED PVC (UPVC) DOWNPIPES & FITTINGS FOR RAINWATER
- AS 1562.1:2018 - DESIGN & INSTALLATION OF SHEET ROOF & WALL CLADDING - METAL
- AS/NZS 1562.3:2006 - DESIGN & INSTALLATION OF SHEET ROOF & WALL CLADDING - PLASTIC
- AS 2049:2002 - ROOF TILES
- AS 2050:2018 - INSTALLATION OF ROOF TILES
- AS 4285:2019 - ROOFLIGHTS

GLAZING

- PART 8 OF THE NCC VOLUME 2, AMENDMENT 1 - BUILDING CODE OF AUSTRALIA 2022 & HOUSING PROVISIONS STANDARD 2022.
- AS 1288:2021 - GLASS IN BUILDINGS - SELECTION & INSTALLATION
- AS 2047:2014 - WINDOWS & EXTERNAL GLAZED DOORS IN BUILDINGS
- AS/NZS 2208:1996 - SAFETY GLAZING MATERIALS IN BUILDINGS

FIRE SAFETY

- PART 9 OF THE NCC VOLUME 2, AMENDMENT 1 - BUILDING CODE OF AUSTRALIA 2022 & HOUSING PROVISIONS STANDARD 2022.
- AS 3786:2014 - SMOKE ALARMS USING SCATTERED LIGHT, TRANSMITTED LIGHT OR IONIZATION

HEALTH & AMENITY

- PART 10 OF THE NCC VOLUME 2, AMENDMENT 1 - BUILDING CODE OF AUSTRALIA 2022 & HOUSING PROVISIONS STANDARD 2022.
- AS/NZS ISO 717.1:2004 - ACOUSTICS - RATING OF SOUND INSULATION IN BUILDINGS & OF BUILDING ELEMENTS - AIRBORNE SOUND INSULATION
- AS ISO 717.2:2004 - ACOUSTICS - RATING OF SOUND INSULATION IN BUILDINGS & OF BUILDING ELEMENTS - IMPACT SOUND INSULATION
- AS 1668.2:2012 - THE USE OF VENTILATION & AIR CONDITIONING IN BUILDINGS - MECHANICAL VENTILATION IN BUILDINGS
- AS 1668.4:2012 - THE USE OF VENTILATION & AIR CONDITIONING IN BUILDINGS - NATURAL VENTILATION OF BUILDINGS
- AS/NZS 1680.0:2009 - INTERIOR LIGHTING - SAFE MOVEMENT
- AS 3740:2021 - WATERPROOFING OF DOMESTIC WET AREAS
- AS 3000:2018 - ELECTRICAL INSTALLATION
- BCA Part 10.8.1, AS4200.1 & AS4200.2 - PLIABLE BUILDING MEMBRANE INSTALLED.

WATERPROOFING

- PART 10.2 OF THE NCC VOLUME 2, AMENDMENT 1 - BUILDING CODE OF AUSTRALIA 2022 & HOUSING PROVISIONS STANDARD 2022
- AS 3740:2021 - WATERPROOFING TO WET AREA
- AS 4654:2012 - EXTERNAL WET AREAS

SAFE MOVEMENT & ACCESS

- PART 11 OF THE NCC VOLUME 2, AMENDMENT 1 - BUILDING CODE OF AUSTRALIA 2022 & HOUSING PROVISIONS STANDARD 2022.
- AS 1428.1:2009 - DESIGN FOR ACCESS & MOBILITY - GENERAL REQUIREMENTS FOR ACCESS - NEW BUILDING WORK
- AS 1657:2018 - FIXED PLATFORMS, WALKWAYS, STAIRWAYS & LADDERS - DESIGN, CONSTRUCTION & INSTALLATION

HANDRAILS & BALUSTRADES

- PART 11.3.3 OF THE NCC VOLUME 2, AMENDMENT 1 - BUILDING CODE OF AUSTRALIA 2022 & HOUSING PROVISIONS STANDARD 2022.
- PART 11.3.4 OF THE NCC VOLUME 2, AMENDMENT 1 - BUILDING CODE OF AUSTRALIA 2022 & HOUSING PROVISIONS STANDARD 2022.
- PART 11.3.5 OF THE NCC VOLUME 2, AMENDMENT 1 - BUILDING CODE OF AUSTRALIA 2022 & HOUSING PROVISIONS STANDARD 2022.
- AS 1170.1:2002 - BALUSTRADE INSTALLATION

PROTECTION OF OPENABLE WINDOW


PART 11.3.7 AND 11.3.8 OF THE NCC VOLUME 2, AMENDMENT 1 - BUILDING CODE OF AUSTRALIA 2022 & HOUSING PROVISIONS STANDARD 2022.

ENERGY EFFICIENCY

- PART 13 OF THE NCC VOLUME 2, AMENDMENT 1 - BUILDING CODE OF AUSTRALIA 2022 & HOUSING PROVISIONS STANDARD 2022 & BASIX CERTIFICATE.

MECHANICAL VENTILATION

- EXHAUST FROM A BATHROOM, SANITARY COMPARTMENT TO DISCHARGE DIRECTLY TO OUTDOOR AIR WITH MINIMUM FLOW RATE OF 25L/S & MAKE-UP AIR VIA OPENINGS TO AN ADJACENT ROOM WITH A FREE AREA OF 14,000 MM². THIS EXHAUST SYSTEM MUST BE INTERLOCKED WITH LIGHT SWITCH AND INCLUDE RUN-ON TIMER SO THAT THE EXHAUST SYSTEM CONTINUES TO OPERATE FOR 10 MINUTES AFTER THE LIGHT SWITCH IS OFF.
- ANY INSTALLED - KITCHEN RANGEHOOD EXHAUST TO DISCHARGE DIRECTLY OR VIA DUCT TO OUTDOOR AIR WITH MINIMUM FLOW RATE OF 40L/S & MAKE-UP AIR VIA OPENINGS TO AN ADJACENT ROOM WITH A FREE AREA OF 14,000 MM².
- LAUNDRY EXHAUST TO DISCHARGE DIRECTLY OR VIA DUCT TO OUTDOOR AIR WITH MINIMUM FLOW RATE OF 40L/S & MAKE-UP AIR VIA OPENINGS TO AN ADJACENT ROOM WITH A FREE AREA OF 14,000 MM².

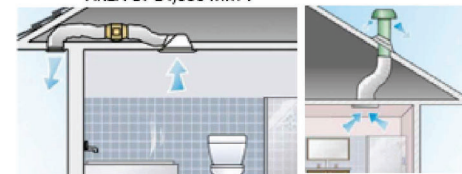

REV	DATE	DESCRIPTION	BY
9	01-07-2026	CDC ISSUE	



THIS DRAWING IS THE EXCLUSIVE PROPERTY OF THE DEVELOPER & THE REPRODUCTION OF ANY PART WITHOUT THE PRIOR WRITTEN CONSENT OF THE DEVELOPER IS A VIOLATION OF APPLICABLE LAWS. IN NO EVENT SHALL THE DEVELOPER BE HELD LIABLE FOR SPECIAL, COLLATERAL, INCIDENTAL OR CONSEQUENTIAL LIABILITY IN CONNECTION WITH THE USE OF THIS DIGITAL DATA ONCE RELEASED FROM THE DEVELOPER'S OFFICE. THIS DRAWING IS TO BE READ & UNDERSTOOD IN CONJUNCTION WITH THE STRUCTURAL, MECHANICAL, ELECTRICAL & / OR OTHER CONSULTANT'S DOCUMENTATION AS MAY BE APPLICABLE TO THE PROJECT PRIOR TO THE START OF ANY WORKS AND FOR ITS DURATION.

PROJECT:

4 BANTAM STREET

LOT 349 4 BANTAM STREET
AUSTRAL 2179

DRAWING TITLE:

GENERAL NOTES

NORTH:

LOT NO:

349

DRAWN BY:
AS

DRAFTED BY:
AS

DATE:

9-09-2026

CHECKED BY:
RH

CLIENT NAME:
Md Reza Razaak Khan & Nusrat Afia Neshat

SCALE:

1 : 2

CDC.02A

ISSUED BY:


CDC ISSUE

REV: 9


CDC.02A

ISSUED BY:

- TERMITE SHEET EXTENDS THROUGH THE ENTIRE MASONRY LEAF AND IS **VISIBLE AT THE FINISHED FACE OF THE WALL.**

 

DAMP-PROOF COURSE (DPC) TO EXTENDS THROUGH THE ENTIRE MASONRY LEAF AND NEED TO BE VISIBLE AT THE FINISHED FACE OF THE WALL FROM OUTSIDE

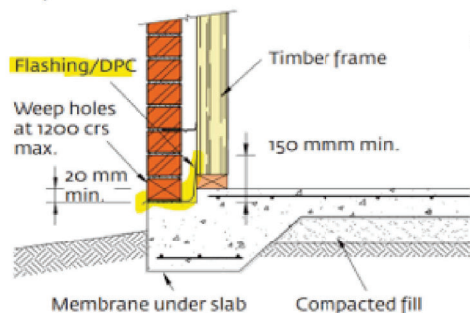

- AS 2601-2001 – DEMOLITION WORK

REFER BELOW DETAILS FOR PLANTER BOX.



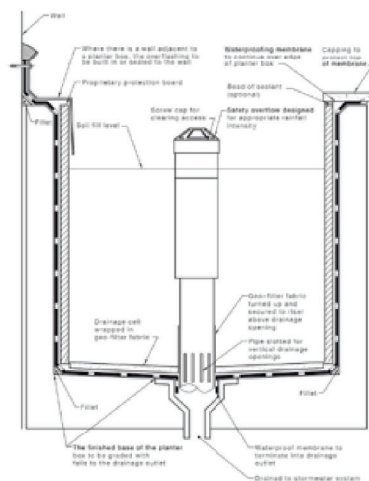


FIGURE 2.17. TYPICAL PLANTER BOX CONSTRUCTION

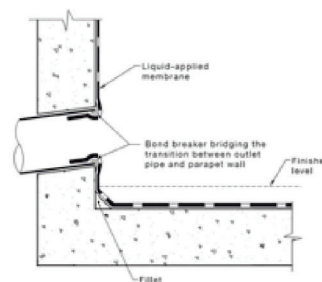

(a) Overflow through parapet

- SURFACE DRAIN & OVERFLOW TO BALCONY

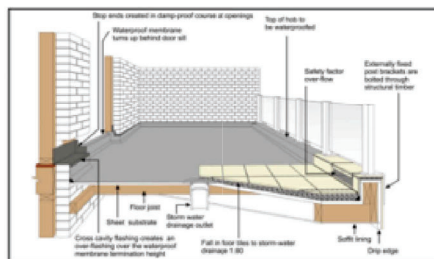


- PART 12.1.1 (H7D2) OF THE NCC VOLUME 2, AMENDMENT 1 - BUILDING CODE OF AUSTRALIA 2022 & HOUSING PROVISIONS STANDARD 2022
- AS 1926 PART 1-2012 – SWIMMING POOLS SAFETY- SAFETY BARRIERS FOR SWIMMING POOLS
- AS 1926 PART 2-2007 - SWIMMING POOL SAFETY- LOCATION OF SAFETY BARRIERS FOR SWIMMING POOLS (INCORPORATING AMENDMENTS 1 AND 2)
- AS 1926 PART 3-2010 – SWIMMING POOL SAFETY- WATER RECIRCULATION SYSTEMS (INCORPORATING AMENDMENT 1)

9	01-07-2026	CDC ISSUE	
REV	DATE	DESCRIPTION	BY




THIS DRAWING IS THE EXCLUSIVE PROPERTY OF THE DEVELOPER & THE REPRODUCTION OF ANY PART WITHOUT THE PRIOR WRITTEN CONSENT OF THE DEVELOPER IS A VIOLATION OF APPLICABLE LAW. IN NO EVENT SHALL THE DEVELOPER BE HELD LIABLE FOR SPECIAL, COLLATERAL, INCIDENTAL OR CONSEQUENTIAL LIABILITY IN CONNECTION WITH THE USE OF THIS DIGITAL DATA ONCE RELEASED FROM THE DEVELOPER'S OFFICE. THIS DRAWING IS TO BE READ & UNDERSTOOD IN CONJUNCTION WITH THE STRUCTURAL, MECHANICAL, ELECTRICAL & / OR ANY OTHER CONSULTANT DOCUMENTATION AS MAY BE APPLICABLE TO THE PROJECT PRIOR TO THE START OF ANY WORKS AND FOR ITS DURATION.

PROJECT:	DRAWING TITLE:	NORTH:	LOT NO:	DATE:	SCALE:	DRAWING No:	REV:
4 BANTAM STREET	GENERAL NOTES		349	9-09-2026			9
			DRAWN BY:	CHECKED BY:	1 : 2	CDC.02B	ISSUED BY:
			AS	RH			
LOT 349 4 BANTAM STREET			DRAFTED BY:	CLIENT NAME:			
AUSTRAL 2179			AS	Md Reza Razaak Khan & Nusrat Afia Neshat			

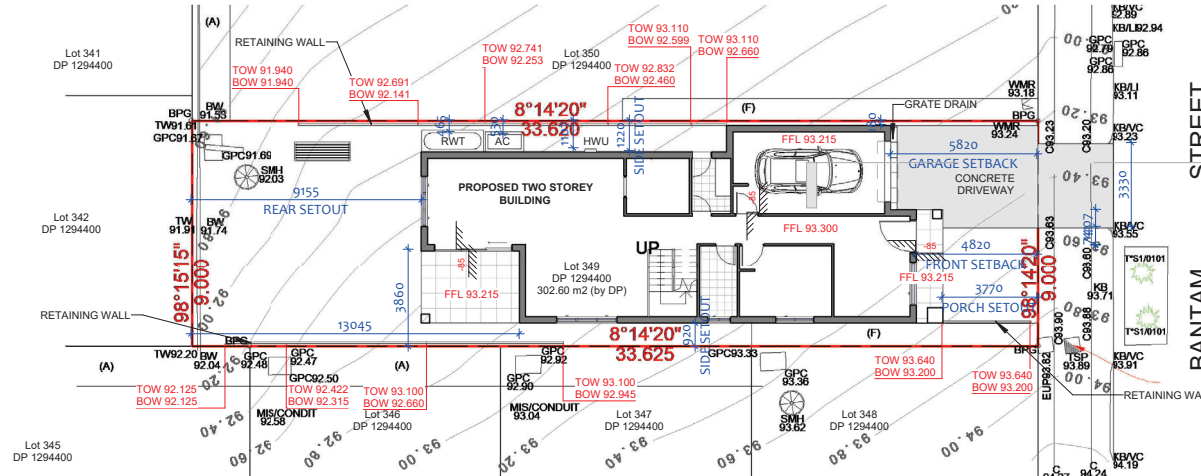

1 SITE PLAN
1 : 200

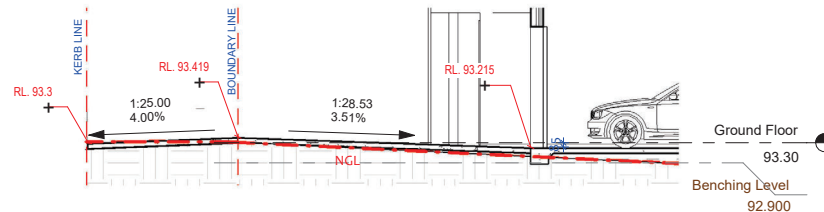

2 DRIVEWAY SECTION
1 : 100

(A) EASEMENT TO DRAIN WATER 1.5 WIDE
(F) EASEMENT FOR ACCESS, MAINTENANCE & OVERHANG 0.9 WIDE

OnBuild Certifiers Pty Ltd	
Reference: 260048	
Area Schedule (Rentable)	
Date: 14/09/2026	
Area	Area
Director/ Principal Certifier	Area
Ground Floor	Area
GFA	94 m ²
GARAGE	20 m ²
ALFRESCO	11 m ²
PORCH	5 m ²
Ground Floor: 4	131 m ²
Level 1	
FFA	89 m ²
VOID	19 m ²
BALCONY	6 m ²
Level 1: 3	114 m ²
Grand total: 7	244 m ²

GREENFIELD HOUSING CODE COMPLIANCE TABLE

DESCRIPTION		COMPLIANCE		COMMENT
ELEMENT	CODE CONTROL	REQUIREMNT	PROPOSED	
LAND ZONE	R2: LOW DENSITY RESIDENTIAL			
LOT NO	LOT 349			
LOT AREA	302.60 m2			
LOT WIDTH	Standard Lot Min. 6m at Building Line facing primary road	6.0m	9 m	YES
HEIGHT	MAX. Height	8.5m	7.5m (MAX.)	YES
FRONT SETBACK	FRONT SET BACK (Min. Setback from Primary Road) For 300-350 sqm. Lot	4.5 m	4.5m	YES
REAR SET BACK (MIN.)	GROUND FLOOR	3m	9.4m	YES
	FIRST FLOOR	6m	9.4 m	
SIDE SET BACK (MIN.)	GROUND FLOOR	0/0.9m	0.18/0.92m	YES
	FIRST FLOOR	1.2/0.9m	1.22/0.92m	
GROSS FLOOR AREA (GFA)	235 sqm.	235.00m2	185 m2	YES
GROSS FLOOR AREA PLAN	GROUND FLOOR		94 m2	
	FIRST FLOOR		89 m2	
GARAGE			20m2	
TOTAL FLOOR AREA			185 m2	
ROOF AREA			165 m2	
PRIVATE OPEN SPACE	6- 10m Lot width	16m2	20 m2	YES
LANDSCAPE AREA	15 % of TOTAL LAND AREA	45.39 m2	100.2 m2	YES

CDC ISSUE

REV	DATE	DESCRIPTION	BY
11	10-07-2026	Building shifted by 270mm rear to comply with articulation	
9	01-07-2026	CDC ISSUE	

RUBY HOMES

THIS DRAWING IS THE EXCLUSIVE PROPERTY OF THE DEVELOPER & THE REPRODUCTION OF ANY PART WITHOUT THE PRIOR WRITTEN CONSENT OF THE DEVELOPER IS A VIOLATION OF APPLICABLE LAWS. IN NO EVENT SHALL THE DEVELOPER BE HELD LIABLE FOR SPECIAL, COLLATERAL, INCIDENTAL OR CONSEQUENTIAL LIABILITY IN CONNECTION WITH THE USE OF THIS DIGITAL DATA ONCE RELEASED FROM THE DEVELOPER'S OFFICE. THIS DRAWING IS TO BE READ & UNDERSTOOD IN CONJUNCTION WITH THE STRUCTURAL, MECHANICAL, ELECTRICAL & / OR ANY OTHER CONSULTANT'S DOCUMENTATION AS MAY BE APPLICABLE TO THE PROJECT PRIOR TO THE START OF ANY WORKS AND FOR ITS DURATION.

PROJECT:
4 BANTAM STREET


LOT 349 4 BANTAM STREET
AUSTRAL 2179

DRAWING TITLE:
LOCATION PLAN
AND SITE PLAN



LOT NO: 349	DATE: 9-09-2026	SCALE: As indicated	DRAWING No: CDC.03	REV: 11
DRAWN BY: AS	CHECKED BY: RH			
DRAFTED BY: AS	CLIENT NAME: Md Reza Razaak Khan & Nusrat Afia Neshat			

OnBuild Construction Ltd
Reference: BOC3540
Date: 09-09-2026
Andrew Solomon
Director/ Principal Designer
BPC3540
IMPORTANT NOTES:
ALL DIMENSIONS AND NOTES ON ALL PLANS MUST BE CHECKED AND VERIFIED BY BUILDERS AND OWNER PRIOR TO COMMENCEMENT OF ANY BUILDING WORKS. TO CLARIFY AND CONFIRM WITH CONSTRUCTION COMPANY FOR DISCREPANCIES IN ALL DOCUMENTS AND PLANS PROVIDED FOR CONSTRUCTION. ANY WORK INDICATED ON THE PLAN BUT NOT IN CONTRACT, VARIATION TO PLANS SPECIFICATIONS MAY NOT BE RESPONSIBILITY OF THE BUILDER. END USER TO VERIFY PLANS CURRENT BCA AND AUSTRALIAN STANDARDS. WINDOWS TO COMPLY WITH 3.9.3.5 OF THE BCA.
Consultant who prepared this document remains responsible for accuracy

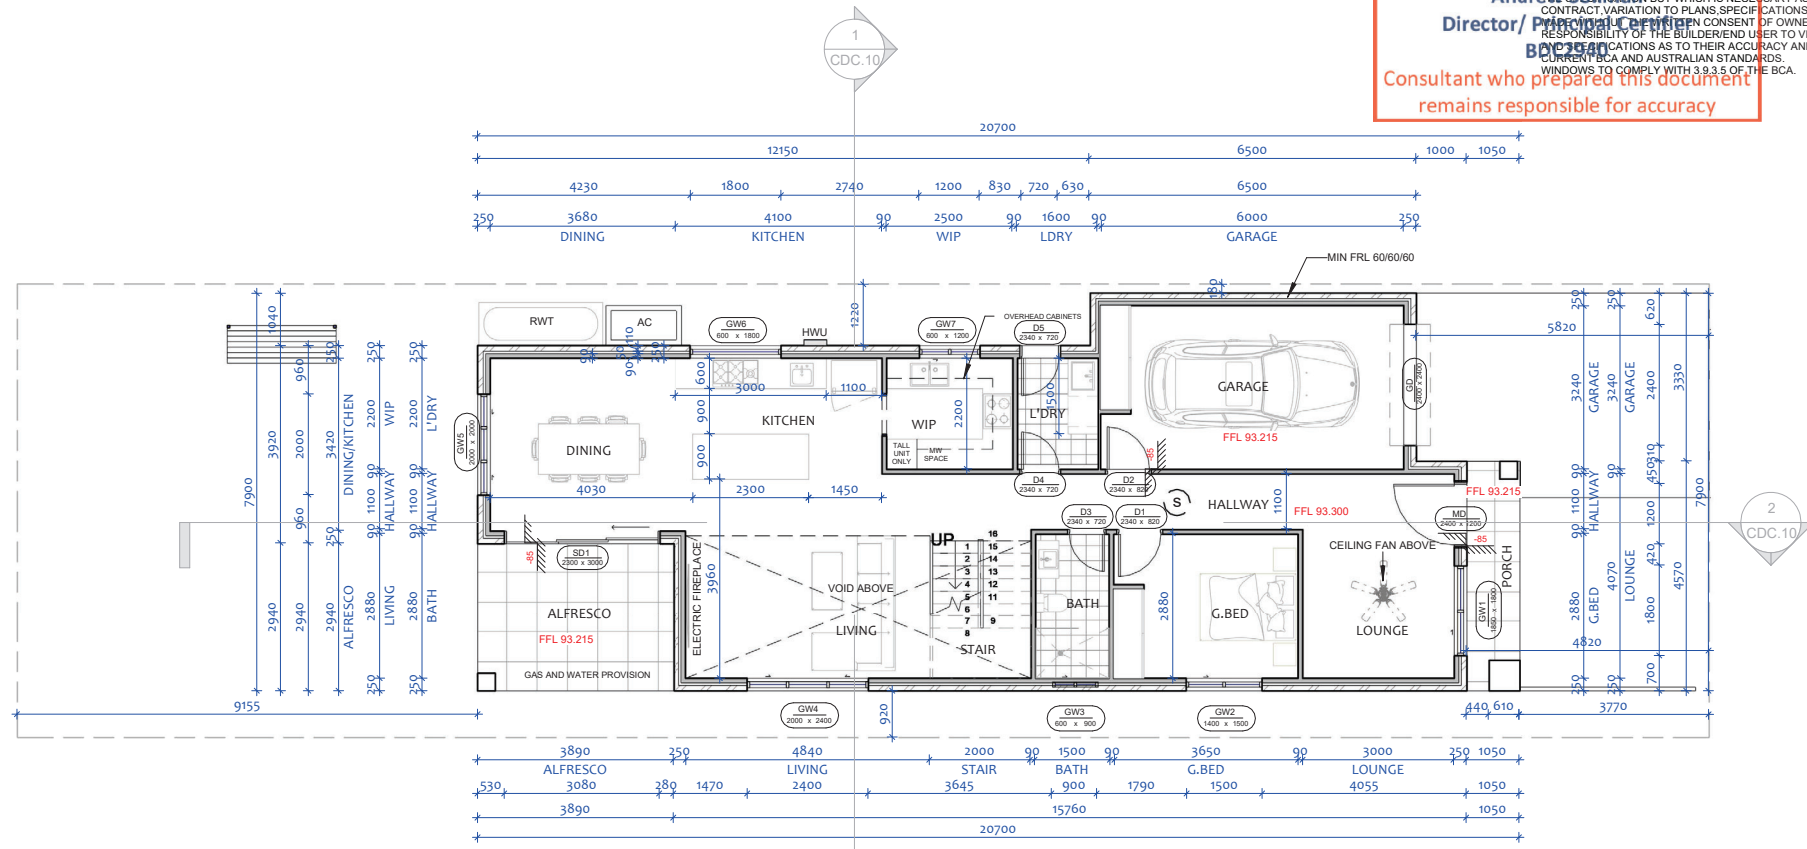

1 Ground Floor
1 : 100

NOTE: PLEASE REFER TO TENDER FOR ALL INCLUSIONS.

REV	DATE	DESCRIPTION	BY
9	01-07-2026	CDC ISSUE	
8	26-06-2026	Bed3 Removed and area adjusted to 270 Sq.m - Ekt	
7	05-06-2026	Hallway Reduced by 100mm on both floors as walls are aligned, Rooms sizes increased by 100mm on West side, Tall unit in Butlers with open microwave space, u shaped counter with overhead cabinets, GW7 Height reduced to accomodate overhead cabinets - Ekt	



THIS DRAWING IS THE EXCLUSIVE PROPERTY OF THE DEVELOPER & THE REPRODUCTION OF ANY PART WITHOUT THE PRIOR WRITTEN CONSENT OF THE DEVELOPER IS A VIOLATION OF APPLICABLE LAWS. IN NO EVENT SHALL THE DEVELOPER BE HELD LIABLE FOR SPECIAL, COLLATERAL, INCIDENTAL OR CONSEQUENTIAL LIABILITY IN CONNECTION WITH THE USE OF THIS DIGITAL DATA ONCE RELEASED FROM THE DEVELOPER'S OFFICE. THIS DRAWING IS TO BE READ & UNDERSTOOD IN CONJUNCTION WITH THE STRUCTURAL, MECHANICAL, ELECTRICAL &/OR ANY OTHER CONSULTANT'S DOCUMENTATION AS MAY BE APPLICABLE TO THE PROJECT PRIOR TO THE START OF ANY WORKS AND FOR ITS DURATION.

PROJECT:
4 BANTAM STREET

LOT 349 4 BANTAM STREET
AUSTRAL 2179

DRAWING TITLE:
GROUND FLOOR PLAN




LOT NO:	DATE:	SCALE:	DRAWING No:	REV:
349	9-09-2026	1 : 100	CDC.05	9
DRAWN BY:	CHECKED BY:	CLIENT NAME:	ISSUED BY:	
AS	RH	Md Reza Razaak Khan & Nusrat Afia Neshat		
DRAFTED BY:	ID			

CDC ISSUE

OnBuild Construction Ltd
Referenced by:
Date: 05-06-2026
Andrew Solomon
Director/ Principal Designer
BPC3540
Consultant who prepared this document
remains responsible for accuracy

IMPORTANT NOTES:
 ALL DIMENSIONS AND NOTES ON ALL PLANS MUST BE CHECKED AND VERIFIED BY BUILDERS AND OWNER PRIOR TO COMMENCEMENT OF ANY BUILDING WORKS. TO CLARIFY AND CONFIRM WITH CONSTRUCTION COMPANY FOR DISCREPANCIES IN ALL DOCUMENTS AND PLANS PROVIDED FOR CONSTRUCTION. ANY WORK INDICATED ON THE PLAN BUT NOT IN CONTRACT, VARIATION TO PLANS SPECIFICATIONS MAY NOT BE RESPONSIBILITY OF THE BUILDER. END USER TO VERIFY PLANS CURRENT BCA AND AUSTRALIAN STANDARDS. WINDOWS TO COMPLY WITH 3.9.3.5 OF THE BCA.

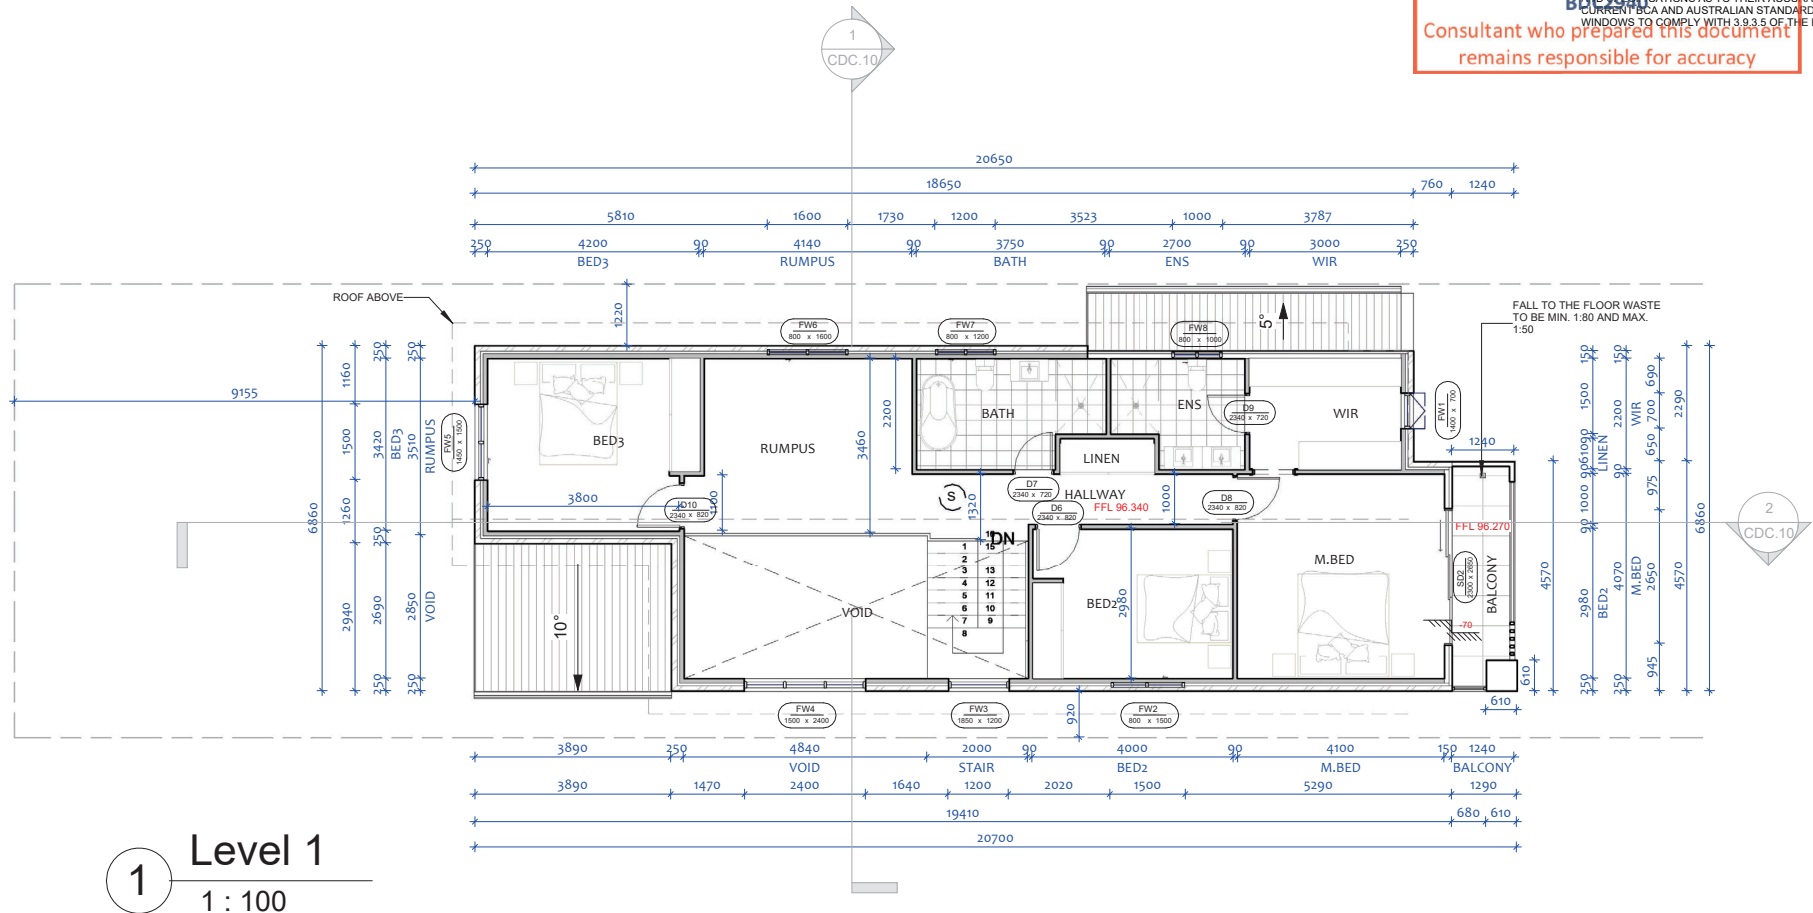

NOTE: PLEASE REFER TO TENDER FOR ALL INCLUSIONS.

REV	DATE	DESCRIPTION	BY
9	01-07-2026	CDC ISSUE	
8	26-06-2026	Bed3 Removed and area adjusted to 270 Sq.m - Ekta	
7	05-06-2026	Hallway Reduced by 100mm on both floors as walls are aligned, Rooms sizes increased by 100mm on West side, Tall unit in Butlers with open microwave space, u shaped counter with overhead cabinets, GW7 Height reduced to accommodate overhead cabinets - Ekta	

RUBY HOMES

THIS DRAWING IS THE EXCLUSIVE PROPERTY OF THE DEVELOPER & THE REPRODUCTION OF ANY PART WITHOUT THE PRIOR WRITTEN CONSENT OF THE DEVELOPER IS A VIOLATION OF APPLICABLE LAWS. IN NO EVENT SHALL THE DEVELOPER BE HELD LIABLE FOR SPECIAL, COLLATERAL, INCIDENTAL OR CONSEQUENTIAL LIABILITY IN CONNECTION WITH THE USE OF THIS DIGITAL DATA ONCE RELEASED FROM THE DEVELOPER'S OFFICE. THIS DRAWING IS TO BE READ & UNDERSTOOD IN CONJUNCTION WITH THE STRUCTURAL, MECHANICAL, ELECTRICAL & / OR ANY OTHER CONSULTANT'S DOCUMENTATION AS MAY BE APPLICABLE TO THE PROJECT PRIOR TO THE START OF ANY WORKS AND FOR ITS DURATION.


PROJECT:
4 BANTAM STREET
LOT 349 4 BANTAM STREET
AUSTRAL 2179

DRAWING TITLE:
FIRST FLOOR
LEVEL



LOT NO:	DATE:	SCALE:	DRAWING No:	REV:
349	9-09-2026	1 : 100	CDC.06	9
DRAWN BY:	CHECKED BY:	DRAFTED BY:	CLIENT NAME:	ISSUED BY:
AS	RH	ID	Md Reza Razaak Khan & Nusrat Afia Neshat	


OnBuild Construction Ltd
Reference:
Date:
Andrew Gillman
Director/
Principal Engineer
Boreham
Consultant who prepared this document
remains responsible for accuracy

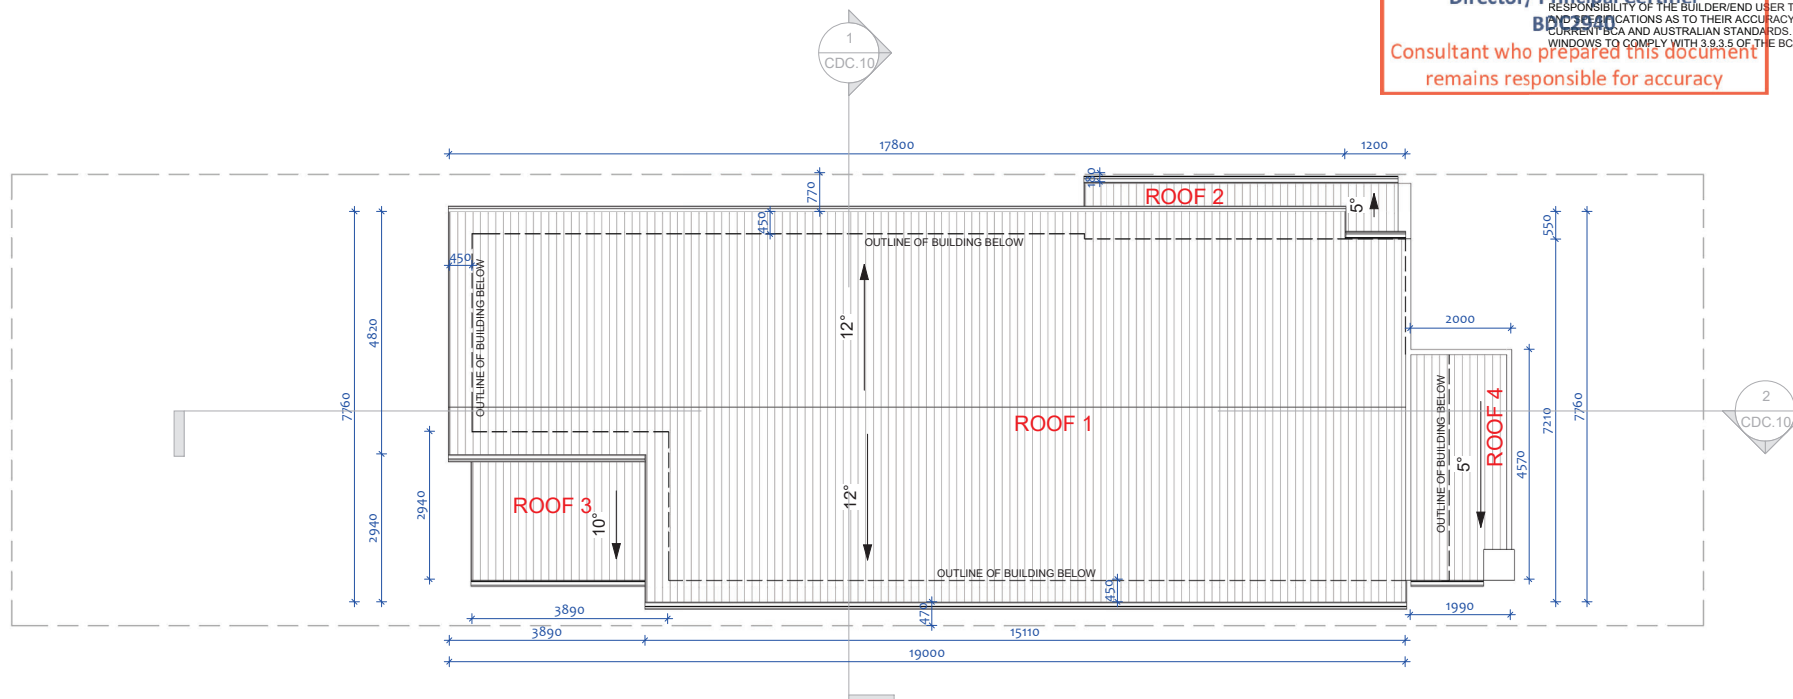

1 ROOF PLAN


Roof Schedule			
Mark	Base Level	Area	Comments
ROOF 2	Level 1	7 m²	COLORBOND(Black or Shades of grey or Neutral colours only)
ROOF 1	CEILING LEVEL	138 m²	COLORBOND(Black or Shades of grey or Neutral colours only)
ROOF 3	Level 1	12 m²	COLORBOND(Black or Shades of grey or Neutral colours only)
ROOF 4	CEILING LEVEL	8 m²	COLORBOND(Black or Shades of grey or Neutral colours only)
Grand total: 4		165 m²	NON REFLECTIVE SURFACE CORRUGATED IRON

9	01-07-2026	CDC ISSUE	
8	26-06-2026	Bed3 Removed and area adjusted to 270 Sq.m - Ekta	
6	16-02-2026	Foam render to all cladding wall-Ek	
REV	DATE	DESCRIPTION	RBY

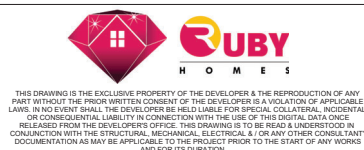


PROJECT:
4 BANTAM STREET
LOT 349 4 BANTAM STREET
AUSTRAL 2179

DRAWING TITLE:
ROOF PLAN

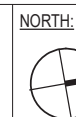


LOT NO: 349	DATE: 9-09-2026	SCALE: 1 : 100	DRAWING No: CDC.07	REV: 9
DRAWN BY: AS	CHECKED BY: RH		ISSUED BY:	
DRAFTED BY:		CLIENT NAME:		
ID		MD Reza Razaak Khan & Nusrat Afia Neshat		

OnBuild Certifiers Pty Ltd
Reference: 260049
Date: 14/09/2026
Andrew Soliman
Director/ Principal Certifier
BDC2940
Consultant who prepared this document
remains responsible for accuracy

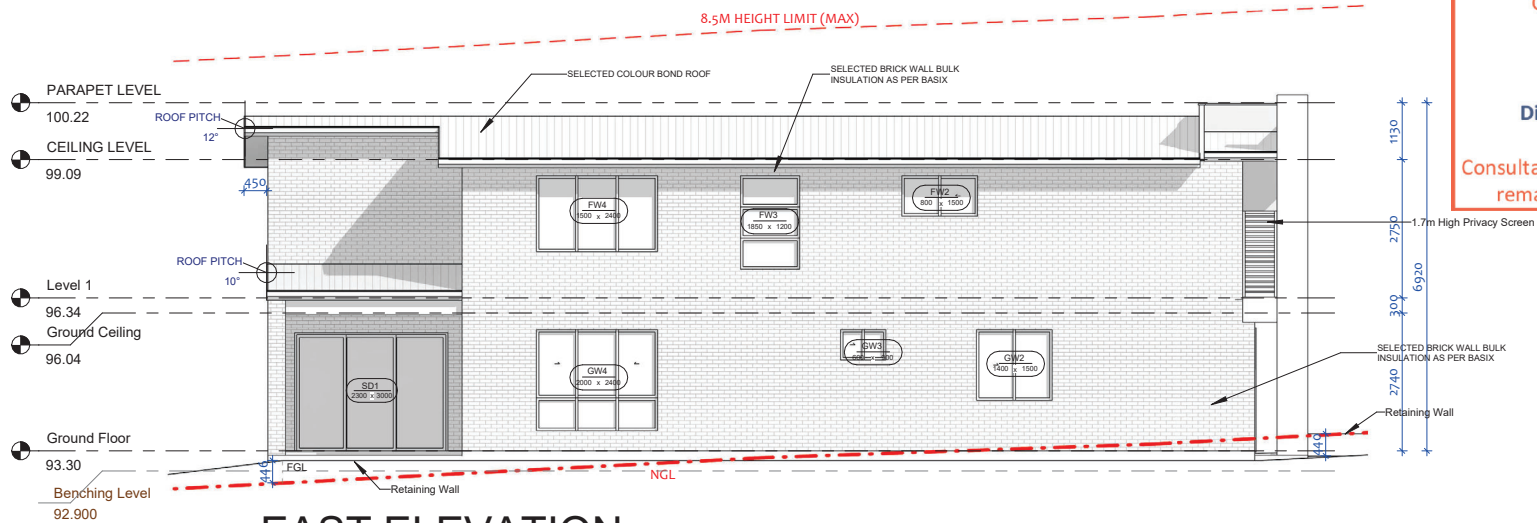

1 EAST ELEVATION
1 : 100

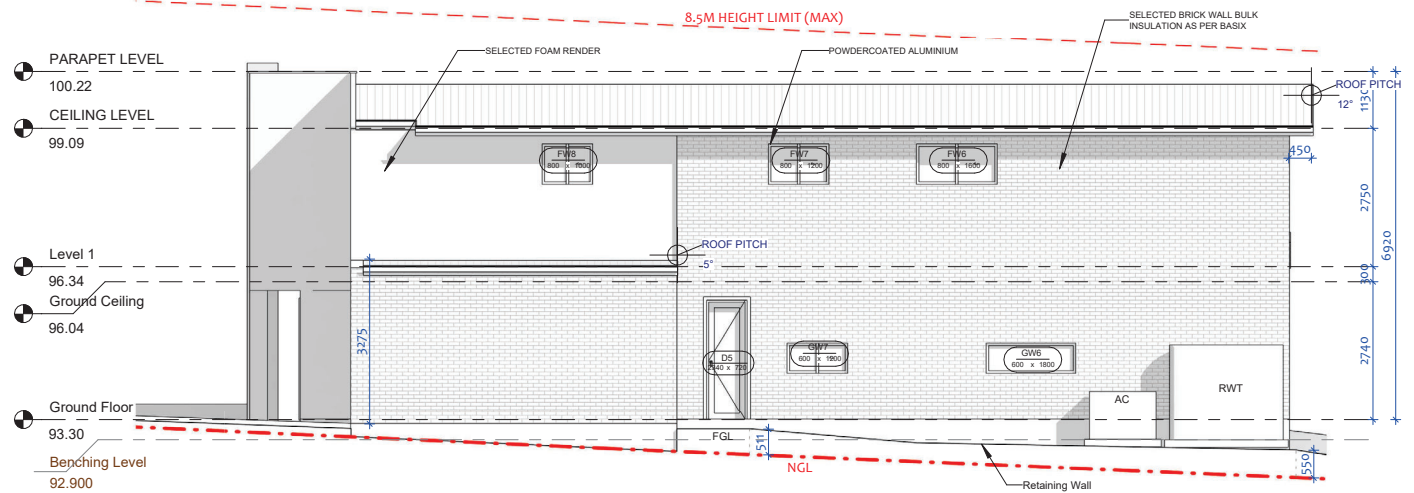

2 WEST ELEVATION
1 : 100

REV	DATE	DESCRIPTION	BY
9	01-07-2026	CDC ISSUE	
8	26-06-2026	Bed3 Removed and area adjusted to 270 Sq.m - Ekta	
6	16-02-2026	Foam render to all cladding wall-Ek	


RUBY HOMES

THIS DRAWING IS THE EXCLUSIVE PROPERTY OF THE DEVELOPER & THE REPRODUCTION OF ANY PART WITHOUT THE PRIOR WRITTEN CONSENT OF THE DEVELOPER IS A VIOLATION OF APPLICABLE LAWS. IN NO EVENT SHALL THE DEVELOPER BE HELD LIABLE FOR SPECIAL, COLLATERAL, INCIDENTAL OR CONSEQUENTIAL LIABILITY IN CONNECTION WITH THE USE OF THIS DIGITAL DATA ONCE RELEASED FROM THE DEVELOPERS OFFICE. THIS DRAWING IS TO BE READ & UNDERSTOOD IN CONJUNCTION WITH THE STRUCTURAL, MECHANICAL, ELECTRICAL & / OR ANY OTHER CONSULTANT'S DOCUMENTATION AS MAY BE APPLICABLE TO THE PROJECT PRIOR TO THE START OF ANY WORKS AND FOR ITS DURATION.

PROJECT:
4 BANTAM STREET


LOT 349 4 BANTAM STREET
AUSTRAL 2179

DRAWING TITLE:
ELEVATION 02


NORTH:

LOT NO:	DATE:	SCALE:	DRAWING No:	REV:
349	9-09-2026	1 : 100	CDC.09	9
DRAWN BY:	CHECKED BY:	DRAFTED BY:	CLIENT NAME:	ISSUED BY:
AS	RH	ID	Md Reza Razaak Khan & Nusrat Afia Neshat	

CDC ISSUE

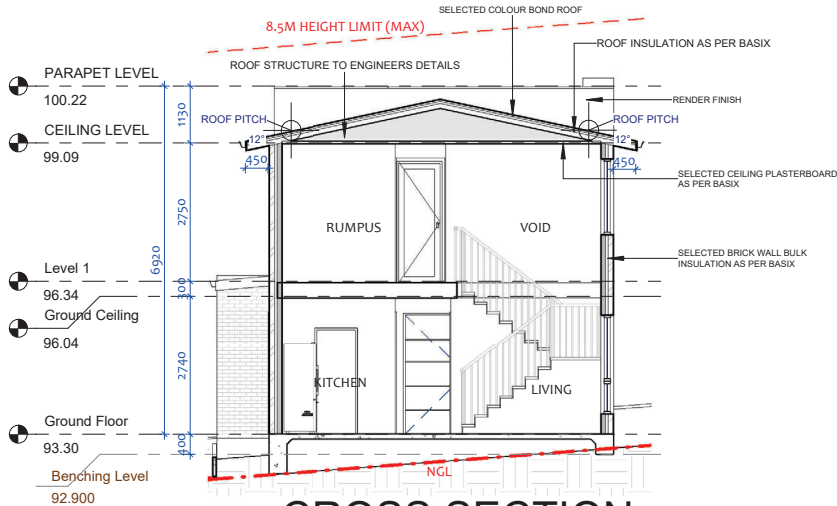

1 CROSS SECTION
1 : 100

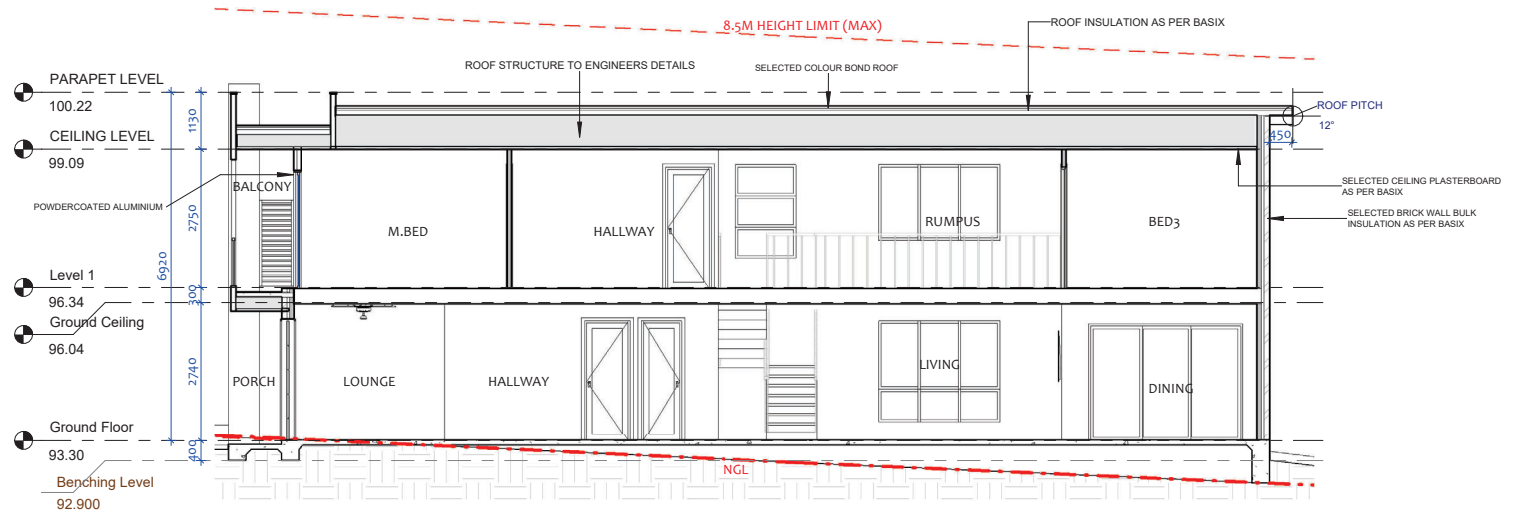

2 LONGITUDINAL SECTION
1 : 100

OnBuild Certifiers Pty Ltd
Reference: 260049
Date: 14/09/2026
Andrew Soliman
Director/ Principal Certifier
BDC2940
Consultant who prepared this document
remains responsible for accuracy

REV	DATE	DESCRIPTION	BY
9	01-07-2026	CDC ISSUE	




PROJECT:	4 BANTAM STREET
LOT 349 4 BANTAM STREET	AUSTRAL 2179

DRAWING TITLE:	SECTIONS
----------------	----------

NORTH:	
--------	--

LOT NO:	349	DATE:	9-09-2026	SCALE:	1 : 100	DRAWING No:	CDC.10	REV:	9
DRAWN BY:	AS	CHECKED BY:	RH					ISSUED BY:	
DRAFTED BY:	AS	CLIENT NAME:	Md Reza Razaak Khan & Nusrat Afia Neshat						


CDC ISSUE

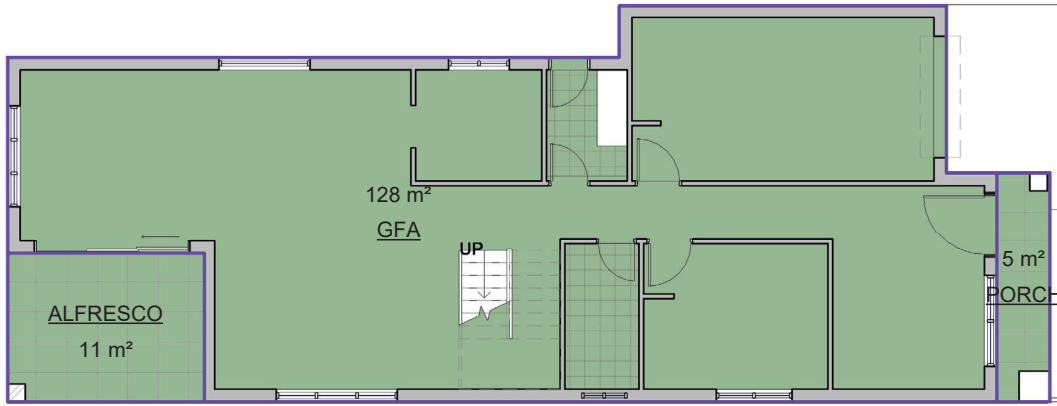

1 Ground Floor
1 : 100

OnBuild Certifiers Pty Ltd
Reference: 260049
Date: 14/09/2026
Andrew Soliman
Director/ Principal Certifier
Area Schedule (Gross Building)
BDC2940
Name Area
Consultant who prepared this document remains responsible for accuracy

Ground Floor	
GFA	128 m²
PORCH	5 m²
ALFRESCO	11 m²
Ground Floor: 3	144 m²
Level 1	
FFA	101 m²
BALCONY	6 m²
VOID	19 m²
Level 1: 3	126 m²
Grand total: 6	270 m²

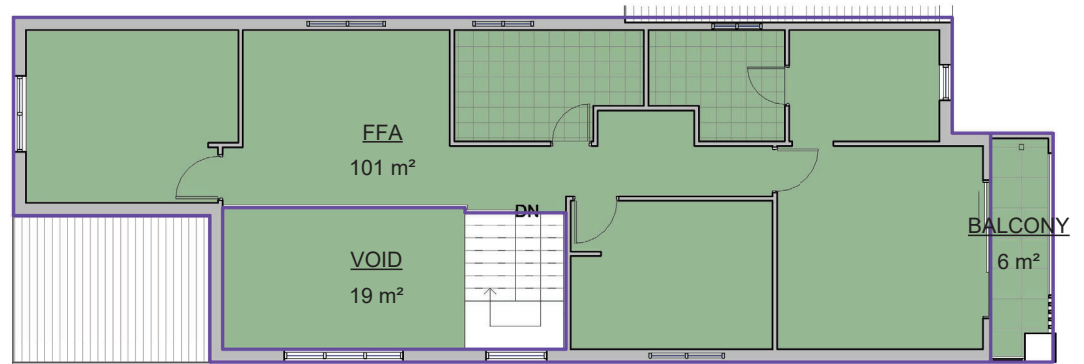

2 Level 1
1 : 100

9	01-07-2026	CDC ISSUE	
8	26-06-2026	Bed3 Removed and area adjusted to 270 Sq.m - Ekta	
7	05-06-2026	Hallway Reduced by 100mm on both floors as walls are aligned, Rooms sizes increased by 100mm on West side, Tall unit in Butlers with open microwave space, u shaped counter with overhead cabinets, GW7 Height reduced to accommodate overhead cabinets - Ekta	
REV	DATE	DESCRIPTION	BY

RUBY HOMES

THIS DRAWING IS THE EXCLUSIVE PROPERTY OF THE DEVELOPER & THE REPRODUCTION OF ANY PART WITHOUT THE PRIOR WRITTEN CONSENT OF THE DEVELOPER IS A VIOLATION OF APPLICABLE LAWS. IN NO EVENT SHALL THE DEVELOPER BE HELD LIABLE FOR SPECIAL, COLLATERAL, INCIDENTAL OR CONSEQUENTIAL LIABILITY IN CONNECTION WITH THE USE OF THIS DIGITAL DATA ONCE RELEASED FROM THE DEVELOPER'S OFFICE. THIS DRAWING IS TO BE READ & UNDERSTOOD IN CONJUNCTION WITH THE STRUCTURAL, MECHANICAL, ELECTRICAL & / OR ANY OTHER CONSULTANTS' DOCUMENTATION AS MAY BE APPLICABLE TO THE PROJECT PRIOR TO THE START OF ANY WORKS AND FOR ITS DURATION.

PROJECT:
4 BANTAM STREET


LOT 349 4 BANTAM STREET
AUSTRAL 2179

DRAWING TITLE:
FLOOR AREA PLAN



LOT NO: 349	DATE: 9-09-2026	SCALE: 1 : 100	DRAWING No: CDC.11	REV: 9
DRAWN BY: AS	CHECKED BY: RH			ISSUED BY:
DRAFTED BY: ID	CLIENT NAME: Md Reza Razaak Khan & Nusrat Afia Neshat			

CDC ISSUE

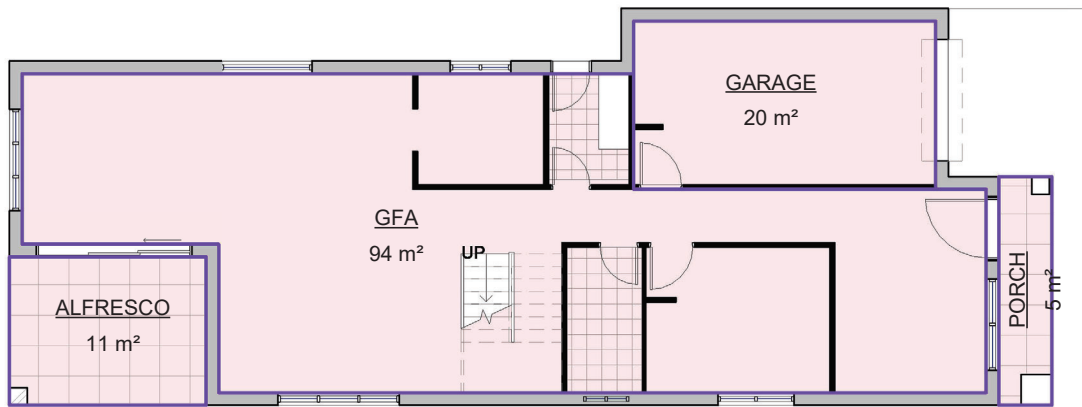

1 Ground Floor
1 : 100

OnBuild Certifiers Pty Ltd	
Reference: 260049	
Date: 14/09/2026	
Andrew Soliman	
Director/ Principal Certifier	
Area Schedule (Rentable)	
89C2948	
Name	Area
Consultant who prepared this document remains responsible for accuracy	

Ground Floor

GFA	94 m²
GARAGE	20 m²
ALFRESCO	11 m²
PORCH	5 m²


Ground Floor: 4 131 m²

Level 1

FFA	89 m²
VOID	19 m²
BALCONY	6 m²

Level 1: 3 114 m²

Grand total: 7 244 m²

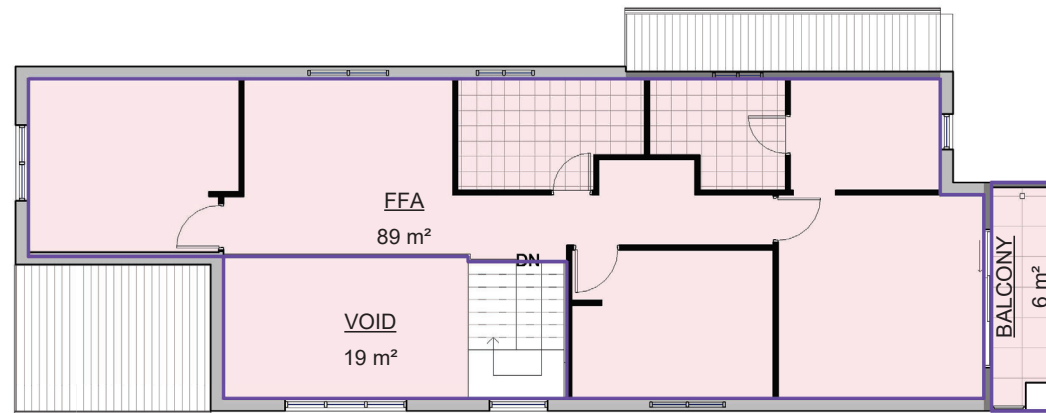

2 Level 1
1 : 100


REV	DATE	DESCRIPTION	BY
9	01-07-2026	CDC ISSUE	



THIS DRAWING IS THE EXCLUSIVE PROPERTY OF THE DEVELOPER & THE REPRODUCTION OF ANY PART WITHOUT THE PRIOR WRITTEN CONSENT OF THE DEVELOPER IS A VIOLATION OF APPLICABLE LAWS. IN NO EVENT SHALL THE DEVELOPER BE HELD LIABLE FOR SPECIAL, COLLATERAL, INCIDENTAL OR CONSEQUENTIAL LIABILITY IN CONNECTION WITH THE USE OF THIS DIGITAL DATA ONCE RELEASED FROM THE DEVELOPER'S OFFICE. THIS DRAWING IS TO BE READ & UNDERSTOOD IN CONJUNCTION WITH THE STRUCTURAL, MECHANICAL, ELECTRICAL & / OR ANY OTHER CONSULTANT'S DOCUMENTATION AS MAY BE APPLICABLE TO THE PROJECT PRIOR TO THE START OF ANY WORKS AND FOR ITS DURATION.

PROJECT:
4 BANTAM STREET
LOT 349 4 BANTAM STREET
AUSTRAL 2179

DRAWING TITLE:
RENTABLE AREA
PLAN

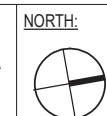

LOT NO:	DATE:	SCALE:	DRAWING No:	REV:
349	9-09-2026	1 : 100	CDC.12	9
DRAWN BY:	CHECKED BY:			ISSUED BY:
AS	RH			
DRAFTED BY:	CLIENT NAME:			
AS	Md Reza Razaak Khan & Nusrat Afia Neshat			

CDC ISSUE

OnBuild Certifiers Pty Ltd
Reference: 260049
Date: 14/09/2026
Andrew Soliman
Director/ Principal Certifier
BDC2940
Consultant who prepared this document
remains responsible for accuracy



	1. RF	2. BR1	3. CD1	4. CR1	5. AL	6. ED	7. GD	8. FAS	9. GUT
	ROOF	MAIN WALLS	FOAM RENDER	ACCENT 1/RENDER	WINDOWS/ BALUSTRADE	MAIN DOOR	GARAGE DOOR	FASCIA	GUTTER
MATERIAL	COLORBOND	BRICK		BRICK	ALUMINIUM	TIMBER	COLORBOND	COLORBOND	COLORBOND
COLOR									

NOTE: ALL COLOURS SPECIFIED ARE INDICATIVE ONLY AND ARE SUBJECT TO VARIATION AND TO AVAILABILITY
ANY DISCREPANCY PLEASE FOLLOW AS PER RENDERED IMAGE

REV	DATE	DESCRIPTION	BY
9	01-07-2026	CDC ISSUE	

RUBY
HOMES

THIS DRAWING IS THE EXCLUSIVE PROPERTY OF THE DEVELOPER & THE REPRODUCTION OF ANY PART WITHOUT THE PRIOR WRITTEN CONSENT OF THE DEVELOPER IS A VIOLATION OF APPLICABLE LAWS. IN NO EVENT SHALL THE DEVELOPER BE HELD LIABLE FOR SPECIAL, COLLATERAL, INCIDENTAL OR CONSEQUENTIAL LIABILITY IN CONNECTION WITH THE USE OF THIS DIGITAL DATA ONCE RELEASED FROM THE DEVELOPER'S OFFICE. THIS DRAWING IS TO BE READ & UNDERSTOOD IN CONJUNCTION WITH THE STRUCTURAL, MECHANICAL, ELECTRICAL & / OR ANY OTHER CONSULTANTS' DOCUMENTATION AS MAY BE APPLICABLE TO THE PROJECT PRIOR TO THE START OF ANY WORKS AND FOR ITS DURATION.

PROJECT:
4 BANTAM STREET

LOT 349 4 BANTAM STREET
AUSTRAL 2179


DRAWING TITLE:
COLOR SCHEDULE

NORTH:

LOT NO:	DATE:	SCALE:	DRAWING No:	REV:
349	9-09-2026	1 : 100	CDC.14	9
DRAWN BY:	CHECKED BY:			ISSUED BY:
AS	RH			
DRAFTED BY:	CLIENT NAME:			
AS	Md Reza Razaak Khan & Nusrat Afia Neshat			

CDC ISSUE

OnBuild Certifiers Pty Ltd
Reference: 260049
Date: 14/09/2026
Andrew Soliman
Director/ Principal Certifier
BDC2940
Consultant who prepared this document
remains responsible for accuracy

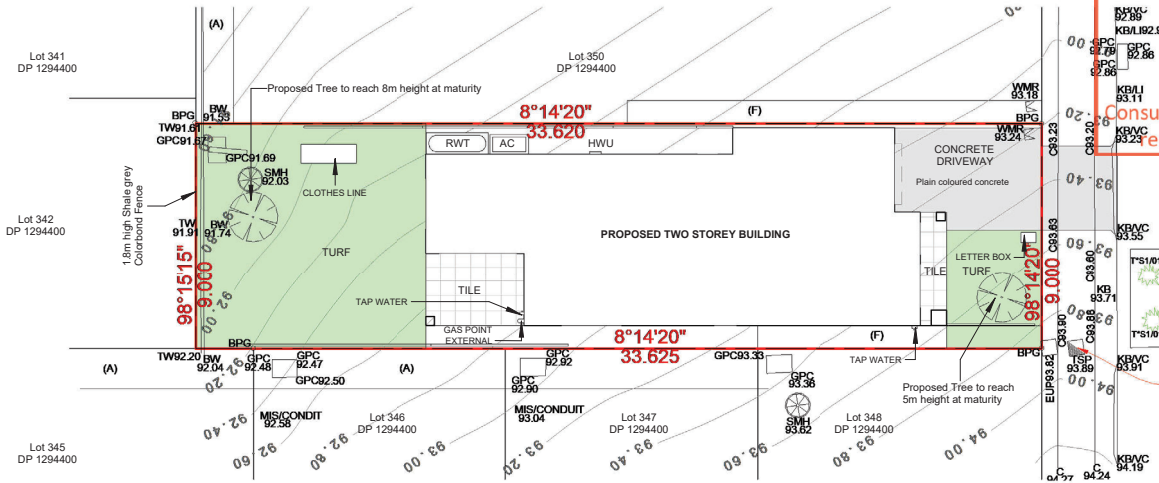

LANDSCAPE PLAN

1 : 200

GENERAL NOTES:

- LANDSCAPE CONTRACTOR TO CHECK DA CONDITIONS AND STAMPED LANDSCAPE PLAN BEFORE COMMENCING WORKS TO ENSURE NO ADDITIONS/AMENDMENTS TO PLAN.
- GARDEN BEDS IN OSD BASIN TO CONSIST OF NON FLOATABLE DECORATIVE GRAVEL.
- REFER TO HYDRAULICS ENGINEERS PLAN FOR OSD DETAILS/FINAL LEVELS.
- MULCHED PLANTING BEDS TO BE A MINIMUM DEPTH OF 75mm AS SELECTED.
- CONTRACTOR'S RESPONSIBILITY TO CHECK AND ADJUST SOIL pH AS REQUIRED.
- PROVIDE TIMBER EDGE AS A MINIMUM BENEATH FENCING/GATES TO DEFINE TURF AND GARDEN BEDS/PATHWAYS. EDGING TO BE PROVIDED TO ALL AREAS WHERE DIFFERING MATERIALS MEET i.e. TURF/GARDEN, TURF/GRAVEL PATH ETC.
- WEED MAT BENEATH GRAVEL PATHWAYS REQUIRED TO LIMIT MUD TRACKING.
- PREMIUM ORGANIC GARDEN MIX TO BE USED.
- ALL PLANTS TO BE HEALTHY AND VIGOROUS.
- CONTRACTOR TO MAKE GOOD TURF ON NATURE STRIP POST CONSTRUCTION.
- CONTRACTOR TO MAKE GOOD TURF ON NATURE STRIP POST CONSTRUCTION.
- DO NOT SCALE ARCHITECTURAL SETOUT FROM LANDSCAPE DRAWING.
- EXISTING TREE SPREAD APPROXIMATE ONLY. REFER TO TREE REPORT WHEN APPLICABLE.
- SITE SURVEY PROVIDED BY OTHERS.
- BUFFALO TURF PREFERRED OVER KIKUYU.

LANDSCAPE BASIX NOTE:

THE APPLICANT MUST PLANT INDIGENEOUS OR LOW WATER USE SPECIES OF VEGETATION THROUGHOUT 15 SQM OF THE SITE.

NOTE: BUILDER RESERVES THE RIGHT NOT TO UNDERTAKE NOR SUPPLY CERTIFICATE FOR OCCUPATION CERTIFICATE.


NOTE: TO AID COMPLIANCE WITH BASIX LEGISLATION, PLANTS (WHERE APPLICABLE) HAVE BEEN SELECTED FROM THE LOCAL CITY/COUNCIL/SHERE PLANT LISTS.

NOTE: LOCATION OF SEWER MAINS/LINES, WATER PIPES, UNDERGROUND ELECTRICITY AND OTHER SERVICES MUST BE OBTAINED PRIOR TO COMMENCEMENT OF ANY WORK ON SITE.

CONTRACTORS NOTE: CALCULATED AREAS DETERMINED BY CAD AND HAVE BEEN ROUNDED UP FOR USE AS A GUIDE ONLY. ALLOW STANDARD PERCENTAGE FOR CUTTING AND WASTAGE. CONFIRM DIMENSIONS AND NUMBERS PRIOR TO QUOTING/ORDERING.


LANDSCAPE AREA

FRONT AREA	17.9 m ²
BACKYARD AREA	82.3 m ²
TOTAL AREA	103 m ²

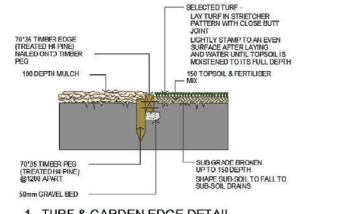

1. TURF & GARDEN EDGE DETAIL

NOTE: ALIGNMENT OF BRICK EDGE SHALL BE EVEN & FREE FROM DIPS AND HILLOCKS.

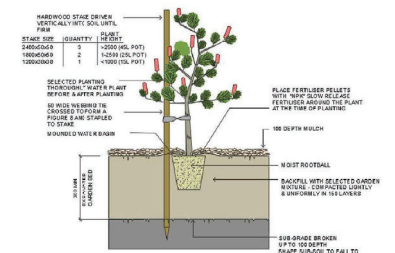

2. TREE & SHRUB PLANTING IN GARDEN BED

NOTE: DO NOT PLANT IN UNSTABLE OR UNUSUAL CONDITIONS SUCH AS SLOPES, WIND EXPOSURE, OR SHAD. SLANT SOIL TO BE THREADED WITH SLANT BRUSH AND UNUSUAL EXPOSURE.

CDC ISSUE

REV	DATE	DESCRIPTION	BY
9	01-07-2026	CDC ISSUE	

RUBY HOMES

THIS DRAWING IS THE EXCLUSIVE PROPERTY OF THE DEVELOPER & THE REPRODUCTION OF ANY PART WITHOUT THE PRIOR WRITTEN CONSENT OF THE DEVELOPER IS A VIOLATION OF APPLICABLE LAWS. IN NO EVENT SHALL THE DEVELOPER BE HELD LIABLE FOR SPECIAL, COLLATERAL, INCIDENTAL OR CONSEQUENTIAL LIABILITY IN CONNECTION WITH THE USE OF THIS DIGITAL DATA. ONCE RELEASED FROM THE DEVELOPER'S OFFICE, THIS DRAWING IS TO BE READ & UNDERSTOOD IN CONJUNCTION WITH THE STRUCTURAL, MECHANICAL, ELECTRICAL & OR ANY OTHER CONSULTANT'S DOCUMENTATION AS MAY BE APPLICABLE TO THE PROJECT PRIOR TO THE START OF ANY WORKS AND FOR ITS DURATION.

PROJECT:
4 BANTAM STREET

LOT 349 4 BANTAM STREET
AUSTRAL 2179

DRAWING TITLE:
LANDSCAPE PLAN

NORTH:



LOT NO: 349	DATE: 9-09-2026	SCALE: 1 : 200	DRAWING No: CDC.15	REV: 9
DRAWN BY: AS	CHECKED BY: RH			ISSUED BY:
DRAFTED BY: AS	CLIENT NAME: MD Reza Razaak Khan & Nusrat Afia Neshat			

ABCB HOUSING PROVISIONS : PART 10.2 WET AREA WATERPROOFING

10.2.1 Wet Areas

- Building elements in wet areas within a building must be protected with a waterproofing system.
- The waterproofing system in (1) must be either waterproof or water resistant in accordance with 10.2.2 to 10.2.6.

10.2.2 Shower Area (enclosed and unenclosed)

- For a shower area with a hob, step-down or level threshold, the following applies:
 - The floor of the shower area must be waterproof, including any hob or step-down (see Figure 10.2.2); and
 - The walls of the shower area must be waterproof not less than 1800 mm above the floor substrate (see Figure 10.2.2).
 - Wall junctions and joints within the shower area must be waterproof not less than 40 mm either side of the junction (see Figure 10.2.2).
 - Wall/floor junctions within the shower area must be waterproof (see Figure 10.2.2).
 - Penetrations within the shower area must be waterproof.
- A shower with a preformed shower base must also comply with the requirements of (1), except for (a) which is not applicable.

Figure 10.2.2: Extent of treatment for shower areas - concrete compressed fibre-cement and fibre-cement sheet floors.

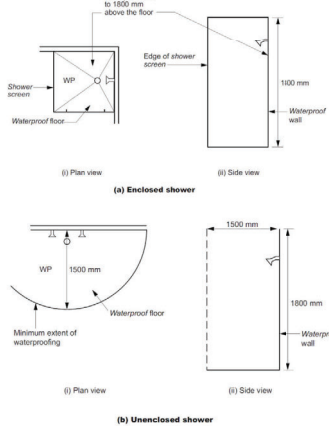


Figure Notes
Wall/floor junction heights are to be as per 10.2.2 to 10.2.6 (as applicable).

Notes
Where a shower is above a bath or spa, use requirements for shower.

10.2.3 Area outside shower area

- For concrete, compressed fibre-cement and fibre-cement sheet flooring, the floor of the room must be water resistant.
- For timber floors including particleboard, plywood and other timber based flooring materials, the floor of the room must be waterproof.
- Wall/floor junctions must be -
 - waterproof, and
 - where a flashing is used, the horizontal leg must be not less than 40 mm.

10.2.4 Areas adjacent to baths and spas without showers

- For areas adjacent to all baths and spas, the following applies:
 - For concrete, compressed fibre-cement and fibre-cement sheet flooring, the floor of the room must be water resistant.
 - For timber floors including particleboard, plywood and other timber based flooring materials, the floor of the room must be waterproof.
 - Tap and spout penetrations must be waterproof where they occur in horizontal surfaces.
- For areas adjacent to non-freestanding baths and spas, the following applies:
 - Walls must be water resistant (see Figure 10.2.4a and Figure 10.2.4b).
 - to a height of not less than 150mm above the vessel, for the extent of the vessel, where the vessel is within 75mm of a wall and
 - for all exposed surfaces below vessel lip.
 - Wall junctions and joints must be water resistant within 150mm above a vessel for the extent of the vessel.
 - Wall/floor junctions must be waterproof for the extent of the vessel (see Figure 10.2.4a and Figure 10.2.4b).
- For inserted baths and spas, the following applies:
 - For floors and horizontal surfaces:
 - Any shelf area adjoining the bath or spa must be waterproof and include a waterstop under the vessel lip.
 - There are no requirements for the floor under a bath or spa.
 - For walls:
 - Waterproof to not less than 150mm above the lip of a bath or spa.
 - There are no requirements for the floor under a bath or spa.
 - For wall junctions and joints, the following applies:
 - Waterproof junctions within 150mm of a bath or spa.
 - There are no requirements for junctions and joints in walls beneath the lip of a bath or spa.
 - Tap and spout penetrations must be waterproof where they occur in horizontal surfaces.

Figure 10.2.4a: Areas adjacent to baths and spas without showers for concrete, compressed fibre-cement and fibre-cement sheet flooring




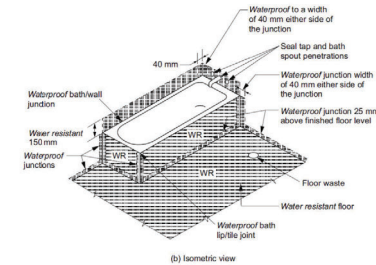



Figure 10.2.4b: Areas adjacent to baths and spas without showers for timber floors including particle-board, plywood and other floor materials

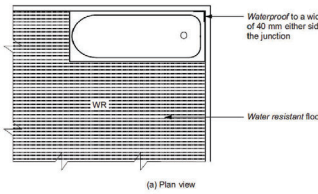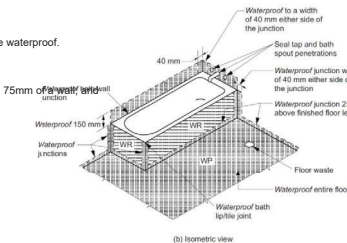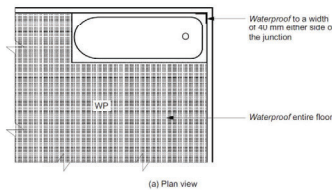

10.2.5 Other areas

- For walls adjoining other types of vessels (not sink, bath or shower), the following applies:
 - Walls must be water resistant to a height of not less than 150mm above the vessel, for the extent of the vessel, where the vessel is within 75 mm of a wall (see Figure 10.2.5).
 - Waterproof wall.
 - Waterproof tap and spout penetrations where they occur in surfaces required to be waterproof or water resistant.
- For laundries and WCs, the following applies:
 - The floor of the room must be water resistant.
 - Wall/floor junctions must be water resistant and where a flashing is used, the horizontal leg must be not less than 40 mm.
- For WCs with a handheld bidet spray installation, the following applies:
 - The floor of the room must be waterproof.
 - Walls must be -
 - waterproof in WC area within a 900 mm radius from the wall connection of the handheld bidet spray device to a height of not less than 150mm above the floor substrate; and
 - water resistant in WC area within a 900 mm radius from the wall connection of the handheld bidet device to not less than 1200 mm above the finished floor level of the WC.
 - Wall junctions within the WC area within 900 mm radius from the wall connection of the handheld bidet spray device must be waterproof.
 - Wall/floor junctions within the WC area within 1000 mm radius from the wall connection of the handheld bidet spray device must be waterproof.
 - Penetrations in the WC area must be waterproof.

Figure 10.2.5: Bath and vessel abutting wall - areas to be protected

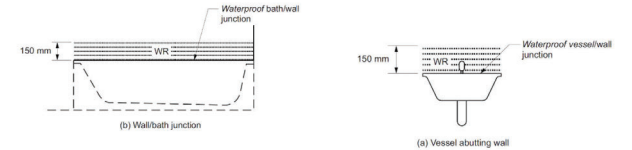

10.2.6 Waterproofing systems

- For the purposes of this Part, a waterproofing system is deemed -
 - waterproof, if it complies with (2); or
 - water resistant, if it complies with (3).
- For a waterproofing system required to be waterproof in accordance with 10.2.2 to 10.2.5, the materials nominated in 10.2.8 must be used.
- For a waterproofing system required to be water resistant in accordance with 10.2.2 to 10.2.5, the materials nominated in 10.2.9 must be used in conjunction with the materials in 10.2.10.

10.2.12 Construction of wet area floors - falls

- Where a floor waste is installed -
- the minimum continuous fall of a floor plane to the waste must be 1:80; and
 - the maximum continuous fall of a floor plane to the waste must be 1:50.

REV	DATE	DESCRIPTION	BY
9	01-07-2026	CDC ISSUE	



RUBY HOMES

THIS DRAWING IS THE EXCLUSIVE PROPERTY OF THE DEVELOPER & THE REPRODUCTION OF ANY PART WITHOUT THE PRIOR WRITTEN CONSENT OF THE DEVELOPER IS A VIOLATION OF APPLICABLE LAWS. IN NO EVENT SHALL THE DEVELOPER BE HELD LIABLE FOR SPECIAL, COLLATERAL, INCIDENTAL OR CONSEQUENTIAL LIABILITY IN CONNECTION WITH THE USE OF THIS DIGITAL DATA ONLY. RELEASED FROM THE DEVELOPERS OFFICE. THIS DRAWING IS TO BE READ & UNDERSTOOD IN CONJUNCTION WITH THE STRUCTURAL, MECHANICAL, ELECTRICAL & / OR ANY OTHER CONSULTANTS' DOCUMENTATION AS MAY BE APPLICABLE TO THE PROJECT PRIOR TO THE START OF ANY WORKS AND FOR ITS DURATION.

PROJECT:	4 BANTAM STREET
LOT 349 4 BANTAM STREET	AUSTRAL 2179

DRAWING TITLE:	WATERPROOFING DETAILS
----------------	-----------------------

NORTH:	
--------	--

LOT NO:	349	DATE:	9-09-2026	SCALE:	1 : 50	DRAWING No:	CDC.16	REV:	9
DRAWN BY:	AS	CHECKED BY:	RH					ISSUED BY:	
DRAFTED BY:	AS	CLIENT NAME:	Md Reza Razaak Khan & Nusrat Afia Neshat						

CDC ISSUE