

FOR CONSTRUCTION

LOT 527 IN DP1310900 LOCATED AT 25 YABUNARU STREET AUSTRAL NSW 2179

Proposed Construction of a New Double-Storey Residential Dwelling with Double Garage and Associated Site Works on a Vacant Allotment



BASIX COMMITMENTS		Certificate number: 1855376S_03 Date of issue: Wednesday, 26 August 2026
WATER		
LANDSCAPE	144m2	
TOILETS	4 STARS	
KITCHEN TAPS	4 STARS	
SHOWER HEADS	5 STAR (>4.5 but <=6 Umin)	
BASIN TAPS	4 STARS	
ALTERNATIVE WATER	1500L RAINWATER TANK	
ROOF WATER TO TANK	182m2	
ALT.WATER USES- TANK	LAUNDRY	
ALT. WATER USES - RETIC	ALL TOILETS + ONE OUTDOOR TAP	
OUTDOOR SPA	NA	
ENERGY		
HOT WATER	GAS INSTANTANEOUS - 5 STAR	
AIR-CON (HEATING)	3 PHASE DUCTED - EER 3.0-3.5	
AIR-CON (COOLING)	3 PHASE DUCTED - EER 3.0-3.5	
VENTILATION - BATHROOM	NONE/ NATURAL VENTILATION	
VENTILATION - KITCHEN	DUCTED - MANUAL SWITCH	
VENTILATION - LAUNDRY	NONE/ NATURAL VENTILATION	
PV SYSTEM	NA	
COOKTOP	GAS	
OVEN	ELECTRIC	
CLOTHES DRYING	OUTDOOR CLOTHESLINE	
LIGHTING	DEDICATED LED	

GENERAL LEGEND	
AC	AIR CONDITIONING UNIT
AL	POWDERCOATED ALUMINIUM DOOR/ WINDOW
BAL	BALUSTRADE TYPE
BG	BOX GUTTER
BR1, BR2, etc.	BRICK FACE TYPE
CAP	METAL CAPPING
CD1, CD2, etc.	WALL CLADDING
CONC.	CONCRETE FLOOR
CPT	CARPET
CRT	CONCRETE ROOF TILES
CR1, CR2, etc.	CEMENT RENDER TYPE/ COLOUR
DP/S	DOWN PIPE
DW	DISH WASHER
ED	ENTRY DOOR
F	FRIDGE
FAS	FASCIA
FET	FEATURE TILE
FT, FT1, FT2, etc.	FLOOR TILES
FW	FLOOR WASTE
GD	GARAGE DOOR
GUT	GUTTER
HWU	HOT WATER UNIT
HYB	HYBRID FLOOR
L	LINEN
MR	METAL ROOF
MW	MICROWAVE OVEN
NGL	NATURAL GROUND LEVEL
OBS	OBSCURED GLASS
P	PANTRY
R	ROBE
RL	REDUCED LEVEL
RWH	RAIN WATER HEAD
RWT	RAIN WATER TANK
S	STORAGE
TOW	TOP OF WALL
TL	TIMBER LAMINATE
WC	WATER CLOSET
WM	WASHING MACHINE
SD	SMOKE DETECTOR

Sheet List		
Sheet No.	Sheet Name	Revision
CC.01	COVER SHEET	6
CC.02	GENERAL NOTES A	6
CC.02B	GENERAL NOTES B	6
CC.03	LOCATION PLAN AND SITE PLAN	6
CC.04A	SEDIMENT CONTROL PLAN	6
CC.04B	SITE ANALYSIS AND WASTE MANAGEMENT PLAN	6
CC.05	GROUND FLOOR PLAN	6
CC.06	FIRST FLOOR LEVEL	6
CC.07	ROOF PLAN	6

Sheet List		
Sheet No.	Sheet Name	Revision
CC.08	ELEVATION 01	6
CC.09	ELEVATION 02	6
CC.10	SECTIONS	6
CC.11	GROSS AREA PLAN	6
CC.12	RENTABLE AREA PLAN	6
CC.13	COLOR SCHEDULE	6
CC.14	LANDSCAPE PLAN	6
CC.15	WATERPROOFING DETAILS	6
CC.16	DRIVEWAY PLAN	5

NOTE : ALL IMAGES ARE FOR ILLUSTRATION ONLY AND ARE SUBJECT TO VARIATION AND TO AVAILABILITY OF MATERIALS.

REV	DATE	DESCRIPTION	BY
6	7-09-2026	CC-ISSUE	
5	26-08-2026	DA - Additional Information	
4	6-08-2026	DA ISSUE	
3	29-04-2026	Brick finish to wall and foam render finish to parapet and cladding wall - Ek	
1	02-04-2026	Bank Set	



THIS DRAWING IS THE EXCLUSIVE PROPERTY OF THE DEVELOPER & THE REPRODUCTION OF ANY PART WITHOUT THE PRIOR WRITTEN CONSENT OF THE DEVELOPER IS A VIOLATION OF APPLICABLE LAWS. IN NO EVENT SHALL THE DEVELOPER BE HELD LIABLE FOR SPECIAL COLLATERAL, INCIDENTAL OR CONSEQUENTIAL LIABILITY IN CONNECTION WITH THE USE OF THIS DIGITAL DATA ONCE RELEASED FROM THE DEVELOPER'S OFFICE. THIS DRAWING IS TO BE READ & UNDERSTOOD IN CONJUNCTION WITH THE STRUCTURAL, MECHANICAL, ELECTRICAL & / OR ANY OTHER CONSULTANT'S DOCUMENTATION AS MAY BE APPLICABLE TO THE PROJECT PRIOR TO THE START OF ANY WORKS AND FOR ITS DURATION.

PROJECT:		DRAWING TITLE:		NORTH:		LOT NO:		DATE:		SCALE:		DRAWING No:		REV:	
25 Yabunaru Street Austral		COVER SHEET				527		8-09-2026		As indicated		CC.01		6	
Lot 527 in DP1310900 at 25 Yabunaru Street Austral NSW 2179						AS		RH						ISSUED BY:	
						SL		Gokul Prasad Prasai & Sunita Karki Prasai							

BUILDING SPECIFICATIONS

**National Construction Code – Volume 2,
Amendment 1 – Building Code of Australia 2022
& Housing Provisions Standard 2022**

SITE PREPARATION

- PART 3.1 OF THE NCC VOLUME 2, AMENDMENT 1 - BUILDING CODE OF AUSTRALIA 2022 & HOUSING PROVISIONS STANDARD 2022.

EARTHWORKS

- TO BE CARRIED OUT IN ACCORDANCE WITH THE REQUIREMENTS OF THE ENVIRONMENTAL PLANNING & ASSESSMENT ACT 1979 AND DEVELOPMENT CONSENT CONDITIONS
- PART 3.2 OF THE NCC VOLUME 2, AMENDMENT 1 - BUILDING CODE OF AUSTRALIA 2022 & HOUSING PROVISIONS STANDARD 2022.
- AS 4678:2002 - EARTH-RETAINING STRUCTURES

DRAINAGE

- PART 3.3 OF THE NCC VOLUME 2, AMENDMENT 1 - BUILDING CODE OF AUSTRALIA 2022 & HOUSING PROVISIONS STANDARD 2022.
- AS/NZS 3500.1:2021 - PLUMBING & DRAINAGE - WATER SERVICES
- AS/NZS 3500.2:2021 - PLUMBING & DRAINAGE - SANITARY PLUMBING & DRAINAGE
- AS/NZS 3500.3:2021 - PLUMBING & DRAINAGE STORMWATER DRAINAGE
- AS/NZS 3500.4:2021 - PLUMBING & DRAINAGE - HEATED WATER SERVICES

STRUCTURAL WORK

- Part 2.2 OF THE NCC VOLUME 2, AMENDMENT 1 - BUILDING CODE OF AUSTRALIA 2022 & HOUSING PROVISIONS STANDARD 2022.
- AS 4100:2020- STEEL STRUCTURES CODES
- AS/NZS 1170.0:2002 – GENERAL PRINCIPLES
- AS/NZS 1170.1:2002 – PARTS 1 PERMANENT, IMPOSED AND OTHER ACTIONS
- AS/NZS 1170.2:2021 – PART 2 WIND ACTIONS
- AS 3700:2018- SAA MASONRY CODE
- AS 1684.3:2021- RESIDENTIAL TIMBER FRAMED CONSTRUCTION

FOOTINGS & SLABS

- PART 4 OF THE NCC VOLUME 2, AMENDMENT 1 - BUILDING CODE OF AUSTRALIA 2022 & HOUSING PROVISIONS STANDARD 2022.
- AS 2159:2009 - PILING - DESIGN & INSTALLATION
- AS 2870:2011 - RESIDENTIAL SLABS & FOOTINGS
- AS 3600:2018 - CONCRETE STRUCTURES

MASONRY

- PART 5 OF THE NCC VOLUME 2, AMENDMENT 1 - BUILDING CODE OF AUSTRALIA 2022 & HOUSING PROVISIONS STANDARD 2022.
- AS 3700:2018 - MASONRY STRUCTURES
- PART 6 OF THE NCC VOLUME 2, AMENDMENT 1 - BUILDING CODE OF AUSTRALIA 2022 & HOUSING PROVISIONS STANDARD 2022.
- AS 1684.2:2021 - RESIDENTIAL TIMBER-FRAMED CONSTRUCTION - NON- CYCLONIC AREAS
- AS 1720.1:2010 - TIMBER STRUCTURES - DESIGN METHODS
- AS 4100:2020 - STEEL STRUCTURES
- AS 3660.1:2014 – TERMITE MANAGEMENT SYSTEM

ROOF & WALL CLADDING

- PART 7 OF THE NCC VOLUME 2, AMENDMENT 1 - BUILDING CODE OF AUSTRALIA 2022 & HOUSING PROVISIONS STANDARD 2022.
- AS 1273:1991 - UNPLASTICIZED PVC (UPVC) DOWNPIPES & FITTINGS FOR RAINWATER
- AS 1562.1:2018 - DESIGN & INSTALLATION OF SHEET ROOF & WALL CLADDING - METAL
- AS/NZS 1562.3:2006 - DESIGN & INSTALLATION OF SHEET ROOF & WALL CLADDING - PLASTIC
- AS 2049:2002 - ROOF TILES
- AS 2050:2018 - INSTALLATION OF ROOF TILES
- AS 4285:2019 – ROOFLIGHTS

GLAZING

- PART 8 OF THE NCC VOLUME 2, AMENDMENT 1 - BUILDING CODE OF AUSTRALIA 2022 & HOUSING PROVISIONS STANDARD 2022.
- AS 1288:2021 - GLASS IN BUILDINGS -SELECTION & INSTALLATION
- AS 2047:2014 - WINDOWS & EXTERNAL GLAZED DOORS IN BUILDINGS
- AS/NZS 2208:1996 - SAFETY GLAZING MATERIALS IN BUILDINGS

FIRE SAFETY

- PART 9 OF THE NCC VOLUME 2, AMENDMENT 1 - BUILDING CODE OF AUSTRALIA 2022 & HOUSING PROVISIONS STANDARD 2022.
- AS 3786:2014 - SMOKE ALARMS USING SCATTERED LIGHT, TRANSMITTED LIGHT OR IONIZATION

HEALTH & AMENITY

- PART 10 OF THE NCC VOLUME 2, AMENDMENT 1 - BUILDING CODE OF AUSTRALIA 2022 & HOUSING PROVISIONS STANDARD 2022.
- AS/NZS ISO 717.1:2004 - ACOUSTICS - RATING OF SOUND INSULATION IN BUILDINGS & OF BUILDING ELEMENTS -AIRBORNE SOUND INSULATION
- AS ISO 717.2:2004 - ACOUSTICS - RATING OF SOUND INSULATION IN BUILDINGS & OF BUILDING ELEMENTS - IMPACT SOUND INSULATION
- AS 1668.2:2012 - THE USE OF VENTILATION & AIR CONDITIONING IN BUILDINGS - MECHANICAL VENTILATION IN BUILDINGS
- AS 1668.4:2012 - THE USE OF VENTILATION & AIR CONDITIONING IN BUILDINGS - NATURAL VENTILATION OF BUILDINGS
- AS/NZS 1680.0:2009 - INTERIOR LIGHTING - SAFE MOVEMENT
- AS 3740:2021 - WATERPROOFING OF DOMESTIC WET AREAS
- AS 3000:2018 – ELECTRICAL INSTALLATION
- BCA Part 10.8.1, AS4200.1 & AS4200.2 – PLIABLE BUILDING MEMBRANE INSTALLED.

WATERPROOFING

- PART 10.2 OF THE NCC VOLUME 2, AMENDMENT 1 - BUILDING CODE OF AUSTRALIA 2022 & HOUSING PROVISIONS STANDARD 2022
- AS 3740:2021- WATERPROOFING TO WET AREA
- AS 4654:2012 – EXTERNAL WET AREAS

SAFE MOVEMENT & ACCESS

- PART 11 OF THE NCC VOLUME 2, AMENDMENT 1 - BUILDING CODE OF AUSTRALIA 2022 & HOUSING PROVISIONS STANDARD 2022.
- AS 1428.1:2009 - DESIGN FOR ACCESS & MOBILITY – GENERAL REQUIREMENTS FOR ACCESS - NEW BUILDING WORK
- AS 1657:2018 - FIXED PLATFORMS, WALKWAYS, STAIRWAYS & LADDERS - DESIGN, CONSTRUCTION & INSTALLATION

HANDRAILS & BALUSTRADE

- PART 11.3.3 OF THE NCC VOLUME 2, AMENDMENT 1 - BUILDING CODE OF AUSTRALIA 2022 & HOUSING PROVISIONS STANDARD 2022.
- PART 11.3.4 OF THE NCC VOLUME 2, AMENDMENT 1 - BUILDING CODE OF AUSTRALIA 2022 & HOUSING PROVISIONS STANDARD 2022.
- PART 11.3.5 OF THE NCC VOLUME 2, AMENDMENT 1 - BUILDING CODE OF AUSTRALIA 2022 & HOUSING PROVISIONS STANDARD 2022.
- AS 1170.1:2002 – BALUSTRADE INSTALLATION

PROTECTION OF OPENABLE WINDOW

PART 11.3.7 AND 11.3.8 OF THE NCC VOLUME 2, AMENDMENT 1 - BUILDING CODE OF AUSTRALIA 2022 & HOUSING PROVISIONS STANDARD 2022.

ENERGY EFFICIENCY

- PART 13 OF THE NCC VOLUME 2, AMENDMENT 1 - BUILDING CODE OF AUSTRALIA 2022 & HOUSING PROVISIONS STANDARD 2022 & BASIX CERTIFICATE.

HEATING APPLIANCES, FIREPLACES, CHIMNEYS AND FLUES

- PART 12.4 OF THE NCC VOLUME 2, AMENDMENT 1 - BUILDING CODE OF AUSTRALIA 2022 & HOUSING PROVISIONS STANDARD 2022.

MECHANICAL VENTILATION

- EXHAUST FROM A BATHROOM, SANITARY COMPARTMENT TO DISCHARGE DIRECTLY TO OUTDOOR AIR WITH MINIMUM FLOW RATE OF 25L/S & MAKE-UP AIR VIA OPENINGS TO AN ADJACENT ROOM WITH A FREE AREA OF 14,000 MM². THIS EXHAUST SYSTEM MUST BE INTERLOCKED WITH LIGHT SWITCH AND INCLUDE RUN-ON TIMER SO THAT THE EXHAUST SYSTEM CONTINUES TO OPERATE FOR 10 MINUTES AFTER THE LIGHT SWITCH IS OFF.
- ANY INSTALLED - KITCHEN RANGEHOOD EXHAUST TO DISCHARGE DIRECTLY OR VIA DUCT TO OUTDOOR AIR WITH MINIMUM FLOW RATE OF 40L/S & MAKE-UP AIR VIA OPENINGS TO AN ADJACENT ROOM WITH A FREE AREA OF 14,000 MM².
- LAUNDRY EXHAUST TO DISCHARGE DIRECTLY OR VIA DUCT TO OUTDOOR AIR WITH MINIMUM FLOW RATE OF 40L/S & MAKE-UP AIR VIA OPENINGS TO AN ADJACENT ROOM WITH A FREE AREA OF 14,000 MM².



CC ISSUE

REV	DATE	DESCRIPTION	BY
6	7-09-2026	CC-ISSUE	
5	26-08-2026	DA - Additional Information	
4	6-08-2026	DA ISSUE	
3	29-04-2026	Brick finish to wall and foam render finish to parapet and cladding wall - Ek	



THIS DRAWING IS THE EXCLUSIVE PROPERTY OF THE DEVELOPER & THE REPRODUCTION OF ANY PART WITHOUT THE PRIOR WRITTEN CONSENT OF THE DEVELOPER IS A VIOLATION OF APPLICABLE LAWS. IN NO EVENT SHALL THE DEVELOPER BE HELD LIABLE FOR SPECIAL COLLATERAL, INCIDENTAL OR CONSEQUENTIAL LIABILITY IN CONNECTION WITH THE USE OF THIS DIGITAL DATA ONCE RELEASED FROM THE DEVELOPER'S OFFICE. THIS DRAWING IS TO BE READ & UNDERSTOOD IN CONJUNCTION WITH THE STRUCTURAL, MECHANICAL, ELECTRICAL & / OR ANY OTHER CONSULTANT'S DOCUMENTATION AS MAY BE APPLICABLE TO THE PROJECT PRIOR TO THE START OF ANY WORKS AND FOR ITS DURATION.

PROJECT:
25 Yabunaru Street
Austral
Lot 527 in DP1310900 at 25 Yabunaru Street Austral NSW 2179

DRAWING TITLE:
GENERAL NOTES A

NORTH:	LOT NO:	DATE:	SCALE:	DRAWING No:	REV:
	527	8-09-2026	1 : 2	CC.02	6
	DRAWN BY:	CHECKED BY:			ISSUED BY:
	AS	RH			
	DRAFTED BY:	CLIENT NAME:			
	SL	Gokul Prasad Prasai & Sunita Karki Prasai			

TERMITE SHEET

- TERMITE SHEET EXTENDS THROUGH THE ENTIRE MASONRY LEAF AND IS VISIBLE AT THE FINISHED FACE OF THE WALL.



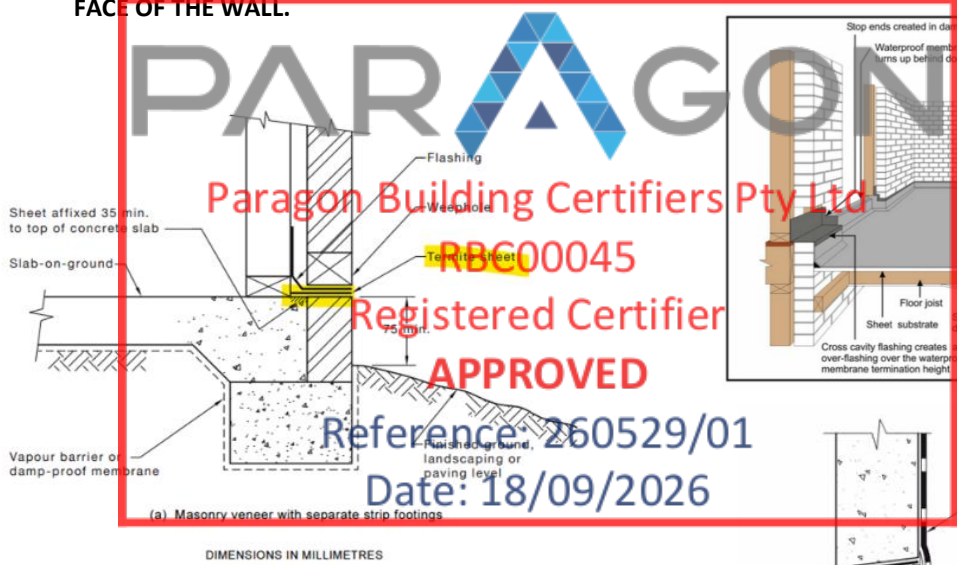


FIGURE 5.5 (in part) TYPICAL SHEET INSTALLATION TO EXTERNAL WALL WITH CONCRETE FLOOR SLAB


OVERFLOW TO BALCONY:

- SURFACE DRAIN & OVERFLOW TO BALCONY

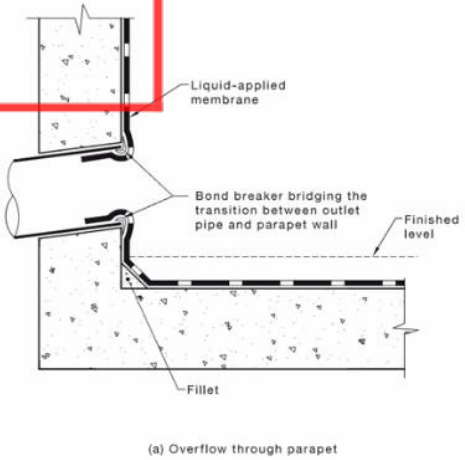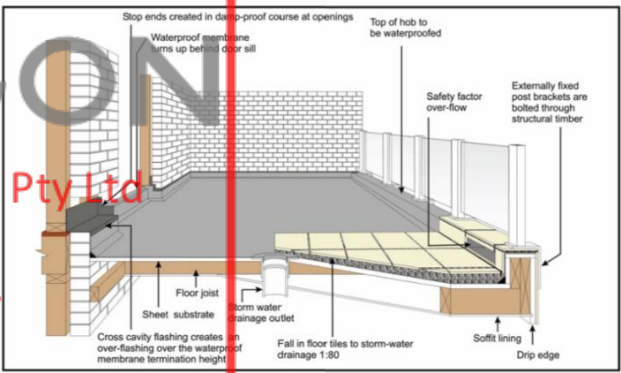

DPC FOR BRICKS

DAMP-PROOF COURSE (DPC) TO EXTENDS THROUGH THE ENTIRE MASONRY LEAF AND NEED TO BE VISIBLE AT THE FINISHED FACE OF THE WALL FROM OUTSIDE

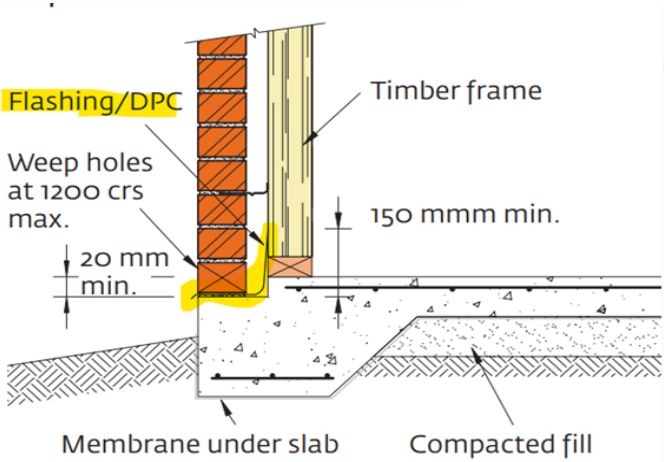

WATERPROOFING

FALL TO FLOOR WASTE TO BE MINIMUM 1:80 TO MAXIMUM 1:50

Figure 10.2.29: Typical membrane termination at drainage outlet



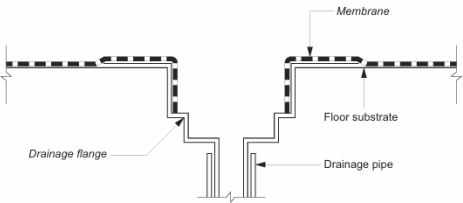


Figure 10.2.24: Typical bathroom door details for whole bathroom waterproofing

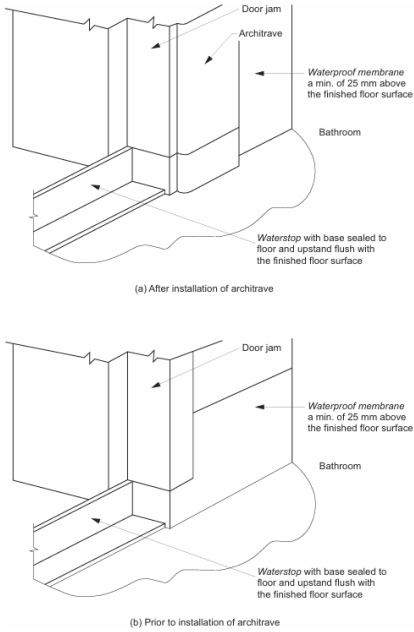


ENCLOSED SHOWER AREA

Figure 10.2.17: Typical hobless construction

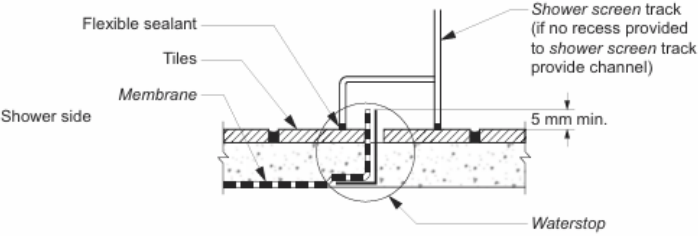


Extent of treatment for shower areas — concrete compressed fibre-cement and fibre-cement sheet floors

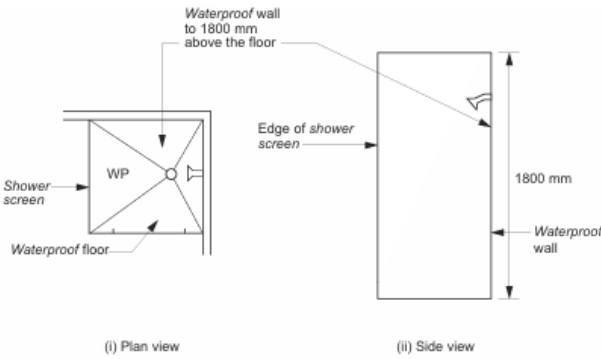

BASIN & BATHTUB:

Figure 10.2.5: Bath and vessel abutting wall — areas to be protected

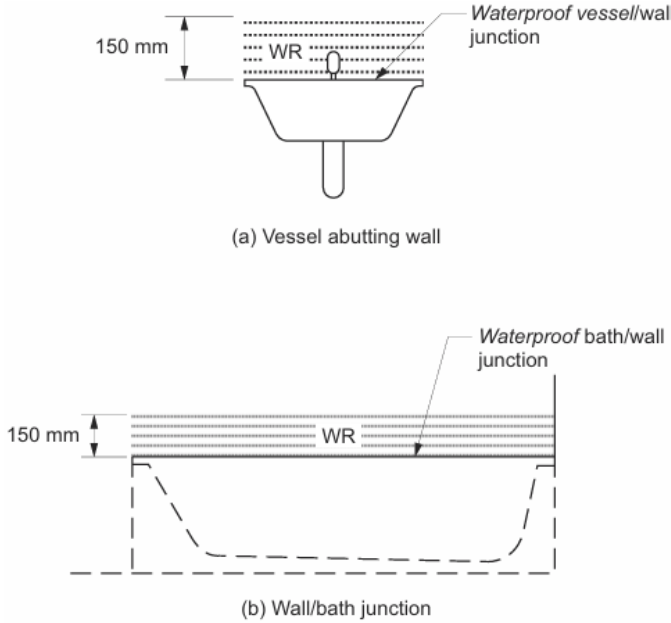

				CC ISSUE			
				LOT NO:	DATE:	SCALE:	DRAWING No: REV: 6
6	7-09-2026	CC-ISSUE		527	8-09-2026		
5	26-08-2026	DA - Additional Information		DRAWN BY:	CHECKED BY:	1 : 2	CC.02B ISSUED BY:
4	6-08-2026	DA ISSUE		AS	RH		
3	29-04-2026	Brick finish to wall and foam render finish to parapet and cladding wall - Ek		DRAFTED BY:	CLIENT NAME:		
REV	DATE	DESCRIPTION	BY	SL	Gokul Prasad Prasai & Sunita Karki Prasai		




THIS DRAWING IS THE EXCLUSIVE PROPERTY OF THE DEVELOPER & THE REPRODUCTION OF ANY PART WITHOUT THE PRIOR WRITTEN CONSENT OF THE DEVELOPER IS A VIOLATION OF APPLICABLE LAWS. IN NO EVENT SHALL THE DEVELOPER BE HELD LIABLE FOR SPECIAL COLLATERAL, INCIDENTAL OR CONSEQUENTIAL LIABILITY IN CONNECTION WITH THE USE OF THIS DIGITAL DATA ONCE RELEASED FROM THE DEVELOPER'S OFFICE. THIS DRAWING IS TO BE READ & UNDERSTOOD IN CONJUNCTION WITH THE STRUCTURAL, MECHANICAL, ELECTRICAL & / OR ANY OTHER CONSULTANT'S DOCUMENTATION AS MAY BE APPLICABLE TO THE PROJECT PRIOR TO THE START OF ANY WORKS AND FOR ITS DURATION.

PROJECT:
25 Yabunaru Street
Austral
Lot 527 in DP1310900 at 25
Yabunaru Street Austral NSW 2179


DRAWING TITLE:
GENERAL NOTES B

NORTH:

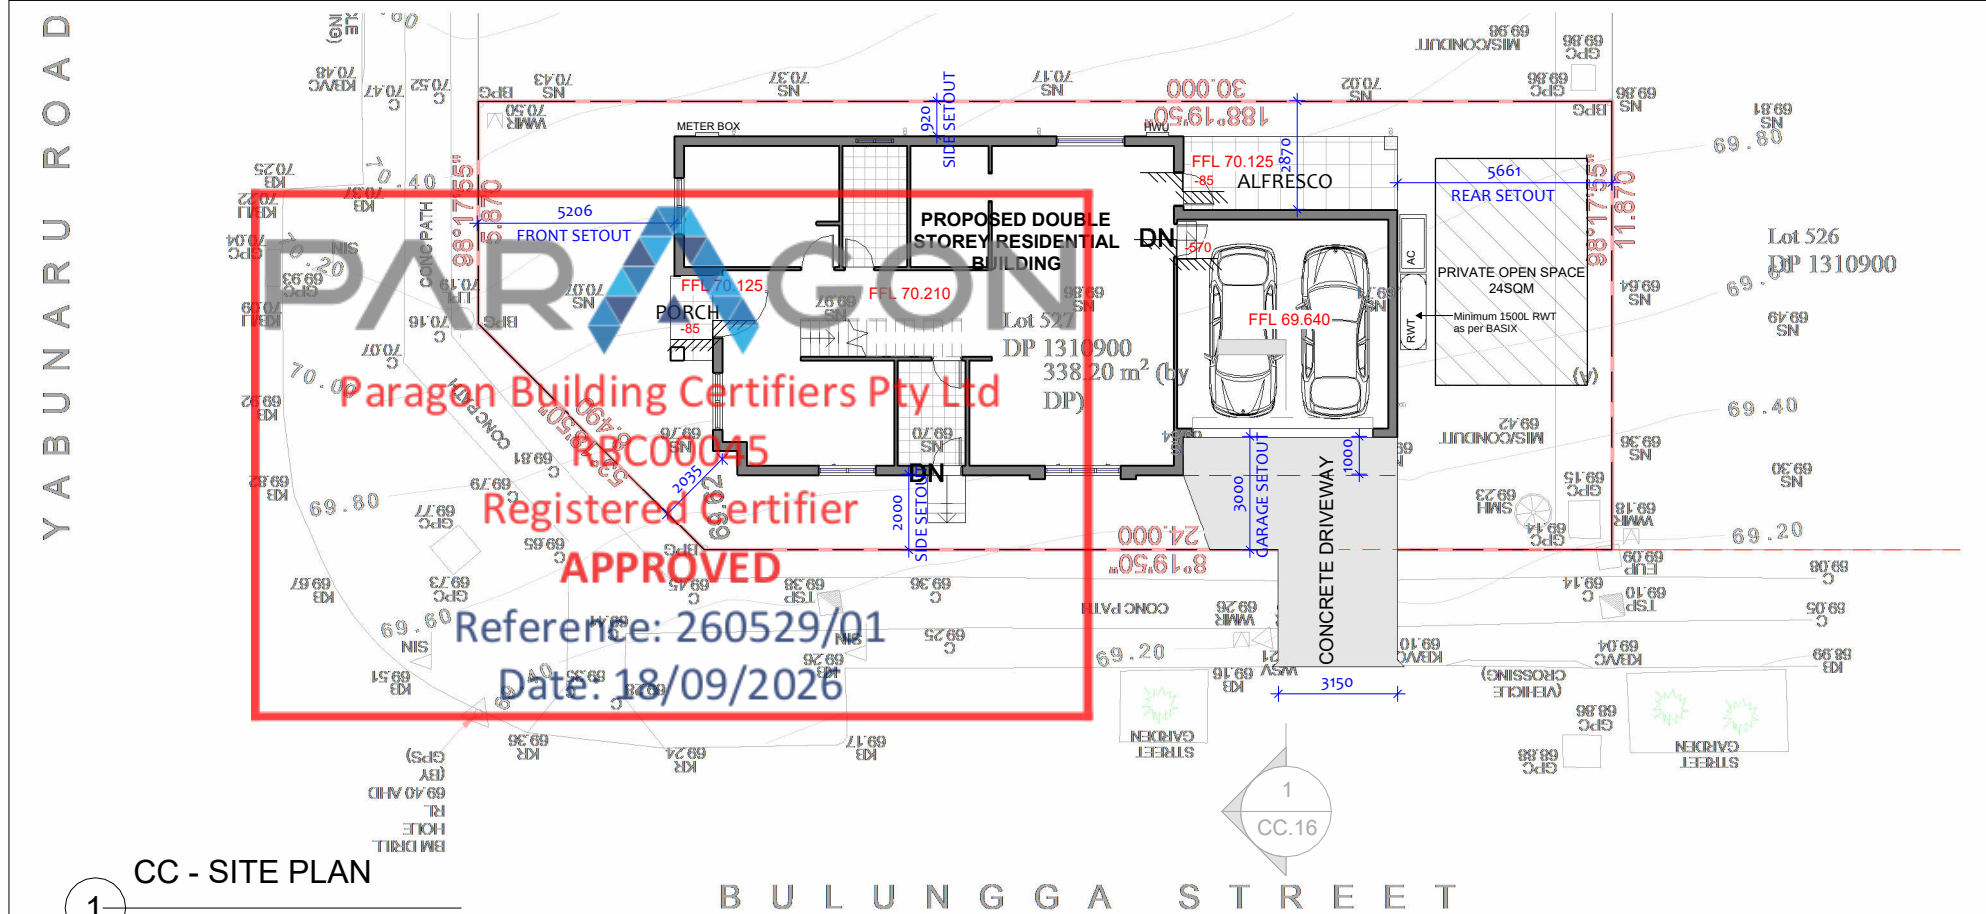

CC - SITE PLAN

1 : 200

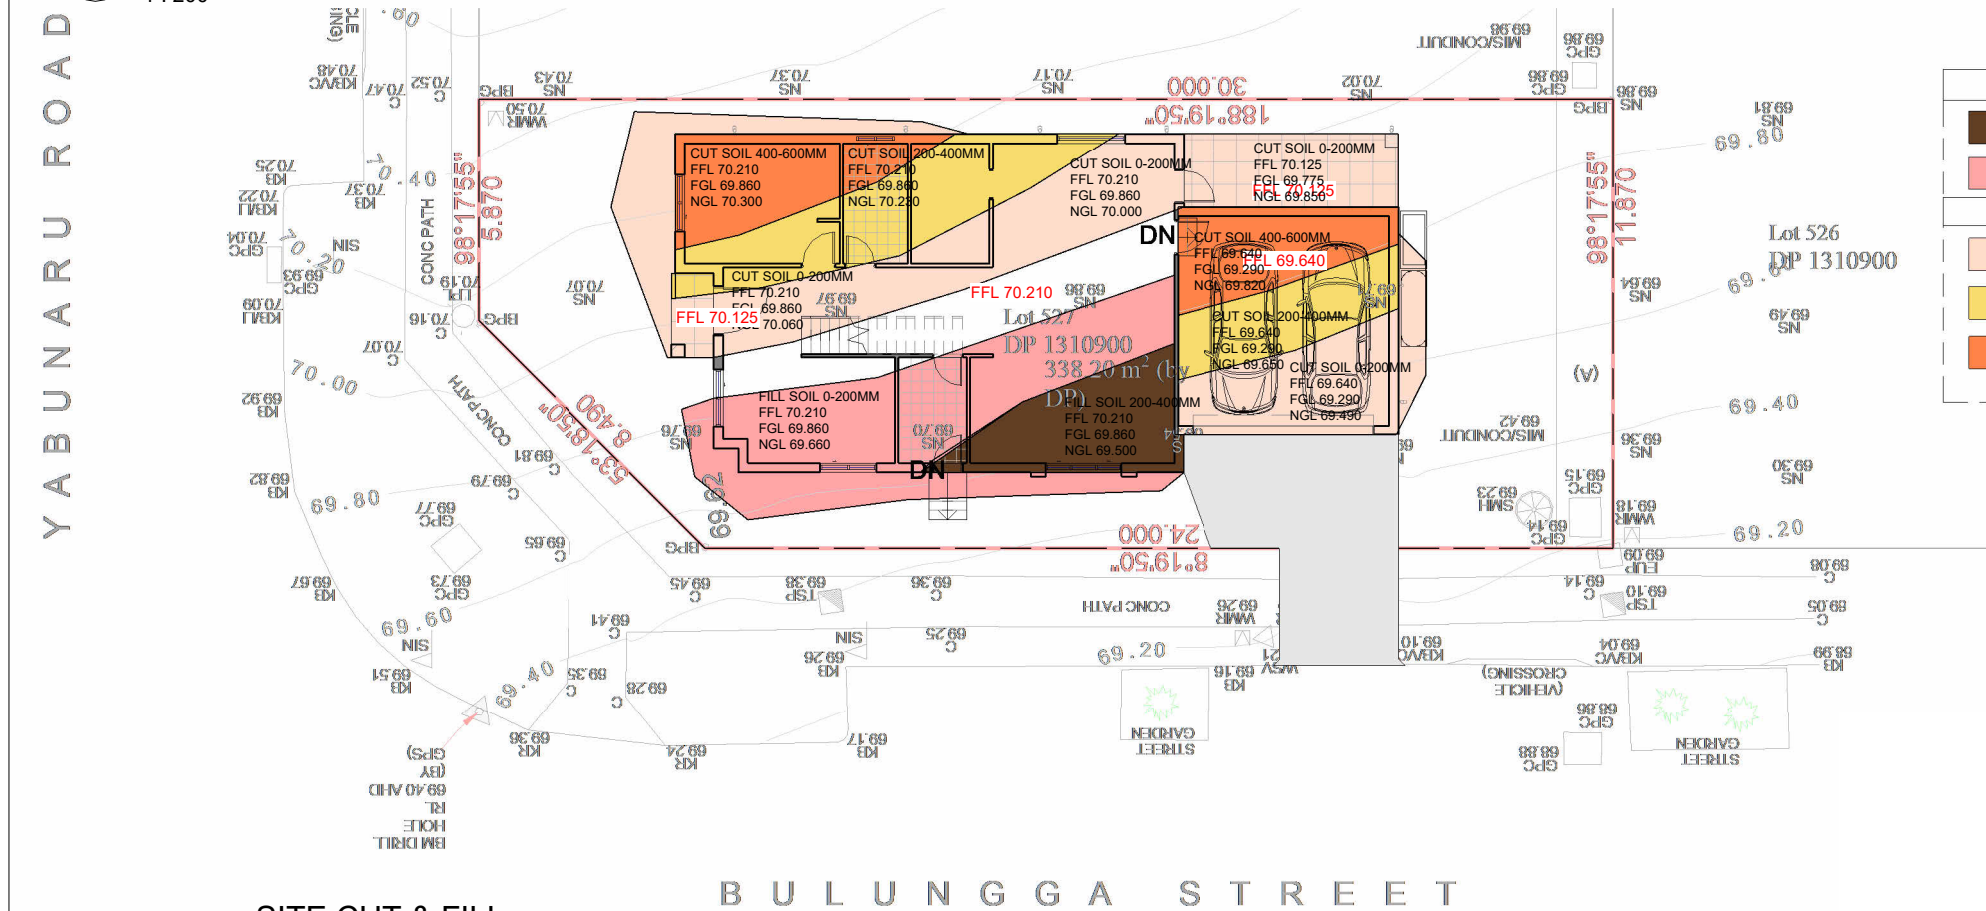

SITE CUT & FILL

2 : 200

COMPLIANCE TABLE

Liverpool Growth Centres Precincts Development Control Plan

DESCRIPTION		COMPLIANCE		COMMENT
ELEMENT	CODE CONTROL	REQUIREMNT	PROPOSED	
LAND ZONE	R2 – Low Density Residential			
LOT NO	LOT 527			
LOT AREA	338.2 m ²			
LOT WIDTH	14.5m	≥ 9m and ≤15m	11m (MAX.)	
HEIGHT	MAX. Height	9m	7.9m (MAX.)	
FRONT SETBACK	4.5m to building facade line; 3.0m to articulation zone;	4.5 m	5.2m	YES
REAR SET BACK (MIN.)	GROUND FLOOR	4m	5.7m	YES
	FIRST FLOOR	6m	11.3m	
SIDE SET BACK (MIN.) Corner Lot	GROUND FLOOR	0.9/2.0m	0.92/2.0m	YES
	FIRST FLOOR	0.9/2.0m	0.92/2.0m	
SITE COVERAGE	GROUND FLOOR	60%	104 m ² (30.75%)	YES
	FIRST FLOOR	40%	86 m ² (25.4%)	
LANDSCAPE AREA	25 % of TOTAL LAND AREA	84.55 m ²	143.5 m ²	YES
Principal Private Open space (PPOS)	>10m Lot width	24m ²	24 m ²	YES
Garages and car parking	Front or rear accessed single, tandem or double garages permitted Triple garages are not permitted.		SIDE DOUBLE GARAGE	

	FILL UPTO 200-400
	FILL UPTO 200
	CUT UPTO 200
	CUT UPTO 200-400
	CUT UPTO 400-600

REV	DATE	DESCRIPTION	BY
6	7-09-2026	CC-ISSUE	
5	26-08-2026	DA - Additional Information	
4	6-08-2026	DA ISSUE	
3	29-04-2026	Brick finish to wall and foam render finish to parapet and cladding wall - Ek	

THIS DRAWING IS THE EXCLUSIVE PROPERTY OF THE DEVELOPER & THE REPRODUCTION OF ANY PART WITHOUT THE PRIOR WRITTEN CONSENT OF THE DEVELOPER IS A VIOLATION OF APPLICABLE LAWS. IN NO EVENT SHALL THE DEVELOPER BE HELD LIABLE FOR SPECIAL COLLATERAL, INCIDENTAL OR CONSEQUENTIAL LIABILITY IN CONNECTION WITH THE USE OF THIS DIGITAL DATA ONCE RELEASED FROM THE DEVELOPER'S OFFICE. THIS DRAWING IS TO BE READ & UNDERSTOOD IN CONJUNCTION WITH THE STRUCTURAL, MECHANICAL, ELECTRICAL & / OR ANY OTHER CONSULTANT'S DOCUMENTATION AS MAY BE APPLICABLE TO THE PROJECT PRIOR TO THE START OF ANY WORKS AND FOR ITS DURATION.


PROJECT:
25 Yabunaru Street
Austral
Lot 527 in DP1310900 at 25 Yabunaru Street Austral NSW 2179

DRAWING TITLE:
LOCATION PLAN AND SITE PLAN

NORTH:

LOT NO: 527	DATE: 8-09-2026	SCALE: As indicated	DRAWING No: CC.03	REV: 6
DRAWN BY: AS	CHECKED BY: RH			ISSUED BY:
DRAFTED BY: SL	CLIENT NAME: Gokul Prasad Prasai & Sunita Karki Prasai			





YABUNARU ROAD

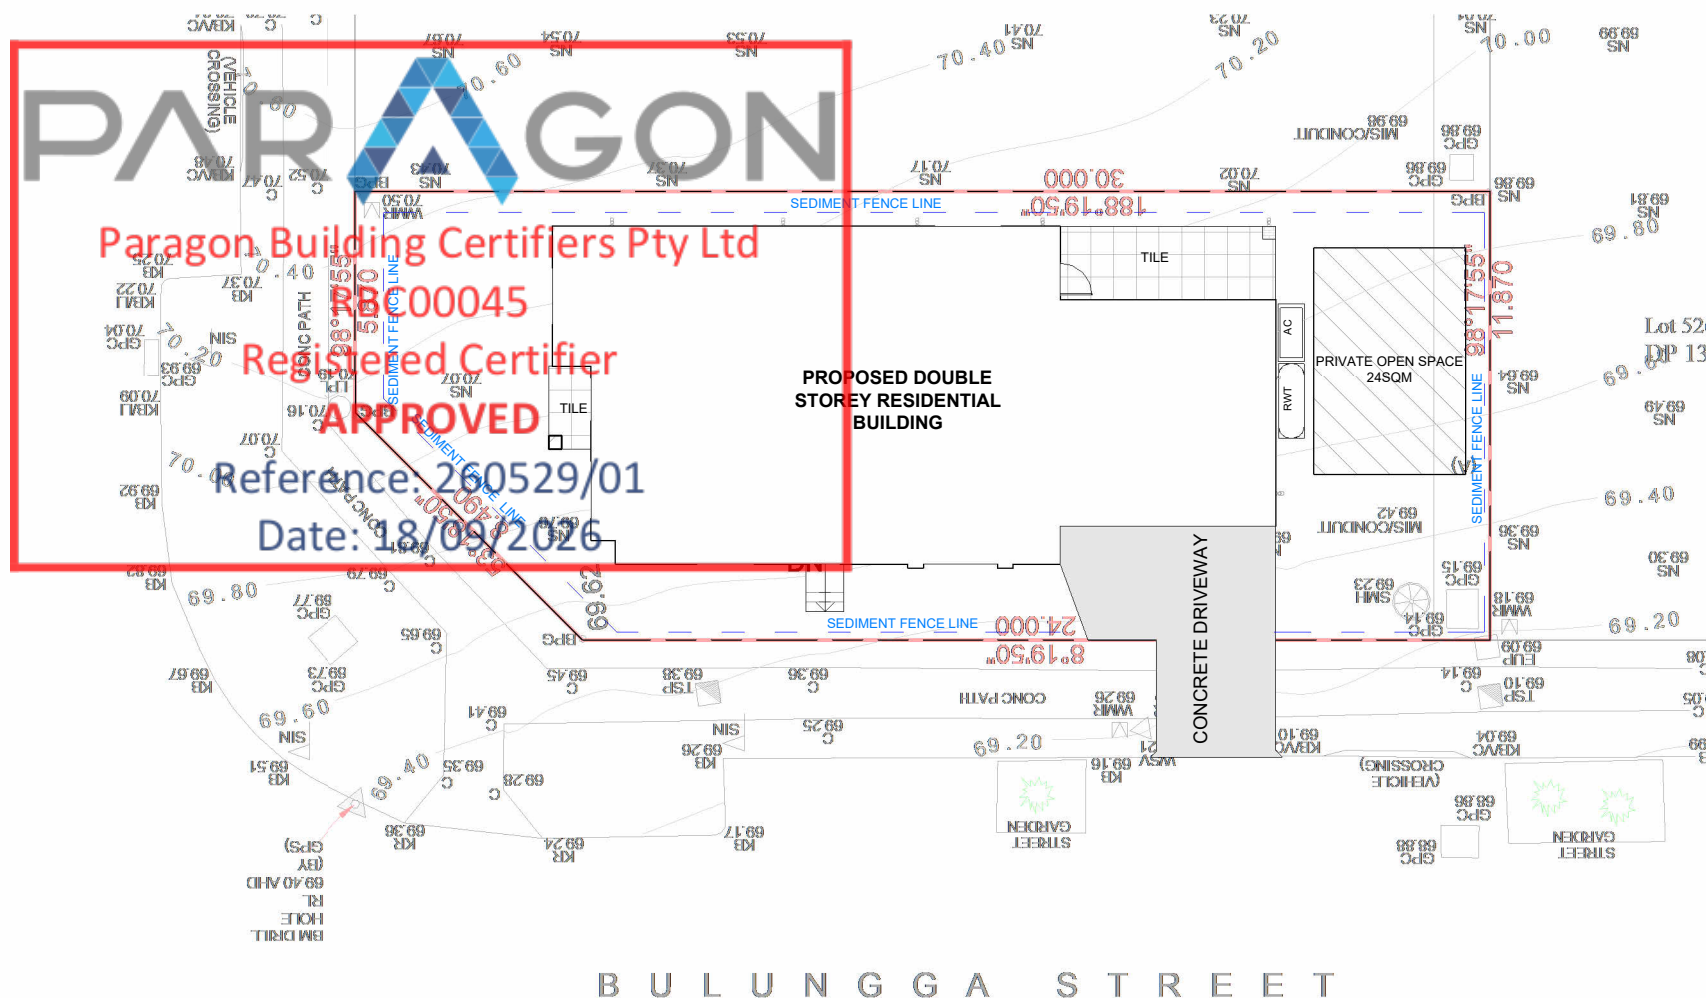

SEDIMENT CONTROL PLAN

1

1 : 200

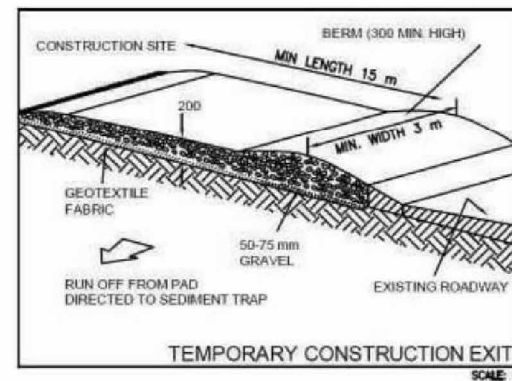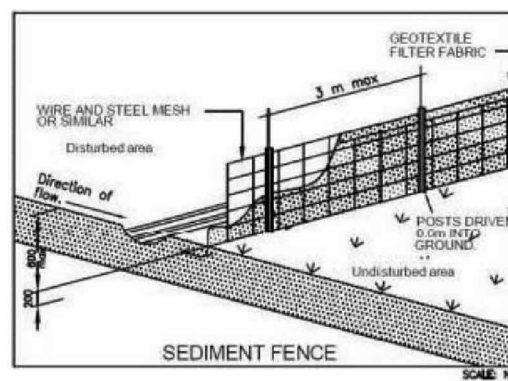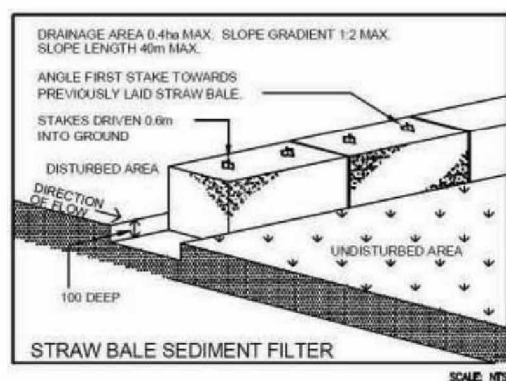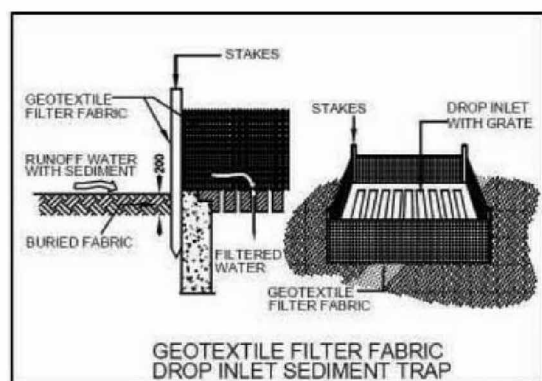

SEDIMENT AND EROSION NOTES:

- THIS PLAN TO BE READ IN CONJUNCTION WITH SEDIMENT AND EROSION CONTROL DETAILS AS ATTACHED.
- THE CONTRACTOR SHALL IMPLEMENT ALL SOIL EROSION AND SEDIMENT CONTROL MEASURES AS NECESSARY AND TO THE SATISFACTION OF COUNCIL PRIOR TO THE COMMENCEMENT AND DURING CONSTRUCTION. NO DISTURBANCE TO THE SITE SHALL BE PERMITTED OTHER THAN IN THE IMMEDIATE AREA OF THE WORK AND NO MATERIAL SHALL BE REMOVED FROM THE SITE WITHOUT COUNCIL'S APPROVAL. ALL SEDIMENT AND EROSION CONTROL DEVICES TO BE INSTALLED AND MAINTAINED IN ACCORDANCE WITH STANDARDS OUTLINED IN NSW DEPARTMENT OF HOUSING "MANAGING URBAN STORMWATER-SOILS AND CONSTRUCTIONS".
- TOPSOIL SHALL BE STRIPPED AND STOCKPILED OUTSIDE HAZARD AREAS SUCH AS DRAINAGE LINES. THIS TOP SOIL IS TO BE RESPIRED LATER ON AREAS TO BE REVEGETATED AND STABILISED ONLY. (I.E ALL FOOTPATHS, BATTERS, SITE REGARDING AREAS, BASINS AND CATCH DRAINS). TOPSOIL SHALL NOT BE RESPIRED ON ANY OTHER AREAS UNLESS SPECIALLY INSTRUCTED BY THE SUPERINTENDENT. IF THEY ARE TO REMAIN FOR LONGER THAN ONE MONTH STOCKPILES SHALL BE PROTECTED FROM EROSION BY COVERING THEM WITH A MULCH AND HYDROSEEDING AND, IF NECESSARY, BY LOCATING BANKS OR DRAINS DOWNSTREAM OF A STOCKPILE TO RETARD SILT LADEN RUNOFF.
- THE CONTRACTOR SHALL REGULARLY MAINTAIN ALL SEDIMENT AND EROSION CONTROL DEVICES AND REMOVE ACCUMULATED SILT FROM SUCH DEVICES SUCH THAT MORE THAN 60% OF THEIR CAPACITY LOST. ALL THE SILTS TO BE PLACED OUTSIDE THE LIMIT OF WORKS. THE PERIOD FOR MAINTAINING THESE DEVICES SHALL BE AT LEAST UNTIL ALL DISTURBED AREAS ARE REVEGETATED AND FURTHER AS MAY BE DIRECTED BY THE SUPERINTENDENT OR COUNCIL.
- LAY TURF STRIP (MIN 300 mm WIDE) ON 100 mm TOPSOIL WITH 1.0 m LONG RETURNS EVERY 6.0m BEHIND ALL KERB AT THE TOP OF ALL BATTERS AND AROUND STRUCTURES IMMEDIATELY AFTER BACKFILLING OR FORMATION.
- THE CONTRACTOR SHALL GRASS SEED ALL DISTURBED AREAS WITH AN APPROVED MIX AS SHOWN AS PRACTICABLE AFTER COMPLETION OF EARTHWORKS AND REGRADING.
- VEHICULAR TRAFFIC SHALL BE CONTROLLED DURING CONSTRUCTION CONFINING ACCESS WHERE POSSIBLE TO NOMINATED STABILISED ACCESS POINTS.
- WHEN ANY DEVICES ARE TO BE HANDED OVER TO COUNCIL, THEY SHALL BE IN CLEAN AND STABLE CONDITION.
- THE CONTRACTOR SHALL IMPLEMENT DUST CONTROL BY REGULAR WETTING DOWN (BUT NOT SATURATING) DISTURBED AREA.
- PROVIDE AND MAINTAIN SILT TRAPS AROUND ALL SURFACE INLET PITS UNTIL CATCHMENT IS REVEGETATED OR PAVED.
- REVEGETATE ALL TRENCHES IMMEDIATELY UPON COMPLETION OF BACKFILLING.
- ALL DRAINAGE PIPE INLETS TO BE CAPPED UNTIL:
 - A) DOWNPIPES CONNECTED
 - B) PITS CONSTRUCTED & PROTECTED WITH SILT BARRIER

SD 6-9 GEOTEXTILE INLET FILTER

- FABRICATE A SEDIMENT BARRIER MADE FROM GEOTEXTILE. REFER SD6-7 FOR DETAILS.
- SUPPORT GEOTEXTILE WITH MESH TIED TO POSTS AT 1 m Ctrs.
- DO NOT COVER INLET WITH GEOTEXTILE.

SITE WORKS NOTES

- ORIGIN OF LEVELS PROVIDED BY SURVEYOR
- THE BUILDER SHALL VERIFY ALL DIMENSIONS AND EXISTING LEVELS ON SITE PRIOR TO THE COMMENCEMENT OF WORK AND ANY DISCREPANCIES SHALL BE REPORTED TO THE SURVEYOR / ENGINEER.
- TOPSOIL SHALL BE STRIPPED FROM THE CONSTRUCTION AREA AND STOCKPILED ON SITE, TO BE LATER SPREAD OR DISPOSED OFF SITE AS DIRECTED BY SUPERVISOR / ENGINEER.
- ALL TRENCH BACKFILL MATERIAL SHALL BE COMPACTED TO THE SAME DENSITY AS THE ADJACENT MATERIAL.
- ALL SERVICE TRENCHES UNDER VEHICULAR PAVEMENTS SHALL BE BACKFILLED WITH SAND OR APPROVED GRANULAR MATERIALS, TO THE UNDERSIDE OF THE PAVEMENT, AND COMPACTED TO 98% STANDARD MAXIMUM DRY DENSITY, IN ACCORDANCE WITH AS 1289E1.1.

SD 5-7 STABILISED SITE ACCESS

- STRIP TOPSOIL AND LEVEL SITE.
- COMPACT SUBGRADE.
- COVER AREA WITH GEOTEXTILE.
- CONSTRUCT 200 mm THICK PAD OVER GEOTEXTILE USING ROADBASE OR 30 mm AGGREGATE. Min 15 m LONG OR TO BUILDING ALIGNMENT. Min 3 m WIDE.
- CONSTRUCT HUMP IMMEDIATELY WITHIN BOUNDARY TO DIVERT WATER TO A SEDIMENT FENCE OR OTHER SEDIMENT TRAP.

CC ISSUE

REV	DATE	DESCRIPTION	BY
6	7-09-2026	CC-ISSUE	
5	26-08-2026	DA - Additional Information	
4	6-08-2026	DA ISSUE	
3	29-04-2026	Brick finish to wall and foam render finish to parapet and cladding wall - Ek	




RUBY
H O M E S

THIS DRAWING IS THE EXCLUSIVE PROPERTY OF THE DEVELOPER AND THE REPRODUCTION OF ANY PART WITHOUT THE PRIOR WRITTEN CONSENT OF THE DEVELOPER IS A VIOLATION OF APPLICABLE LAWS. IN NO EVENT SHALL THE DEVELOPER BE HELD LIABLE FOR SPECIAL COLLATERAL, INCIDENTAL OR CONSEQUENTIAL LIABILITY IN CONNECTION WITH THE USE OF THIS DIGITAL DATA ONCE RELEASED FROM THE DEVELOPER'S OFFICE. THIS DRAWING IS TO BE READ & UNDERSTOOD IN CONJUNCTION WITH THE STRUCTURAL, MECHANICAL, ELECTRICAL & / OR ANY OTHER CONSULTANT'S DOCUMENTATION AS MAY BE APPLICABLE TO THE PROJECT PRIOR TO THE START OF ANY WORKS AND FOR ITS DURATION.

PROJECT:
25 Yabunaru Street
Austral
Lot 527 in DP1310900 at 25
Yabunaru Street Austral NSW 2179

DRAWING TITLE:
**SEDIMENT CONTROL
PLAN**

NORTH:

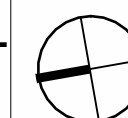

LOT NO:	DATE:	SCALE:	DRAWING No:	REV:
527	8-09-2026	As indicated	CC.04A	6
DRAWN BY:	CHECKED BY:	CLIENT NAME:	ISSUED BY:	
AS	RH	Gokul Prasad Prasai & Sunita Karki Prasai		
DRAFTED BY:	SL			



Paragon Building Certifiers Pty Ltd

RBC00045


Registered Certifier

APPROVED

Reference: 260529/01

Date: 18/09/2026

YABUNARU STREET

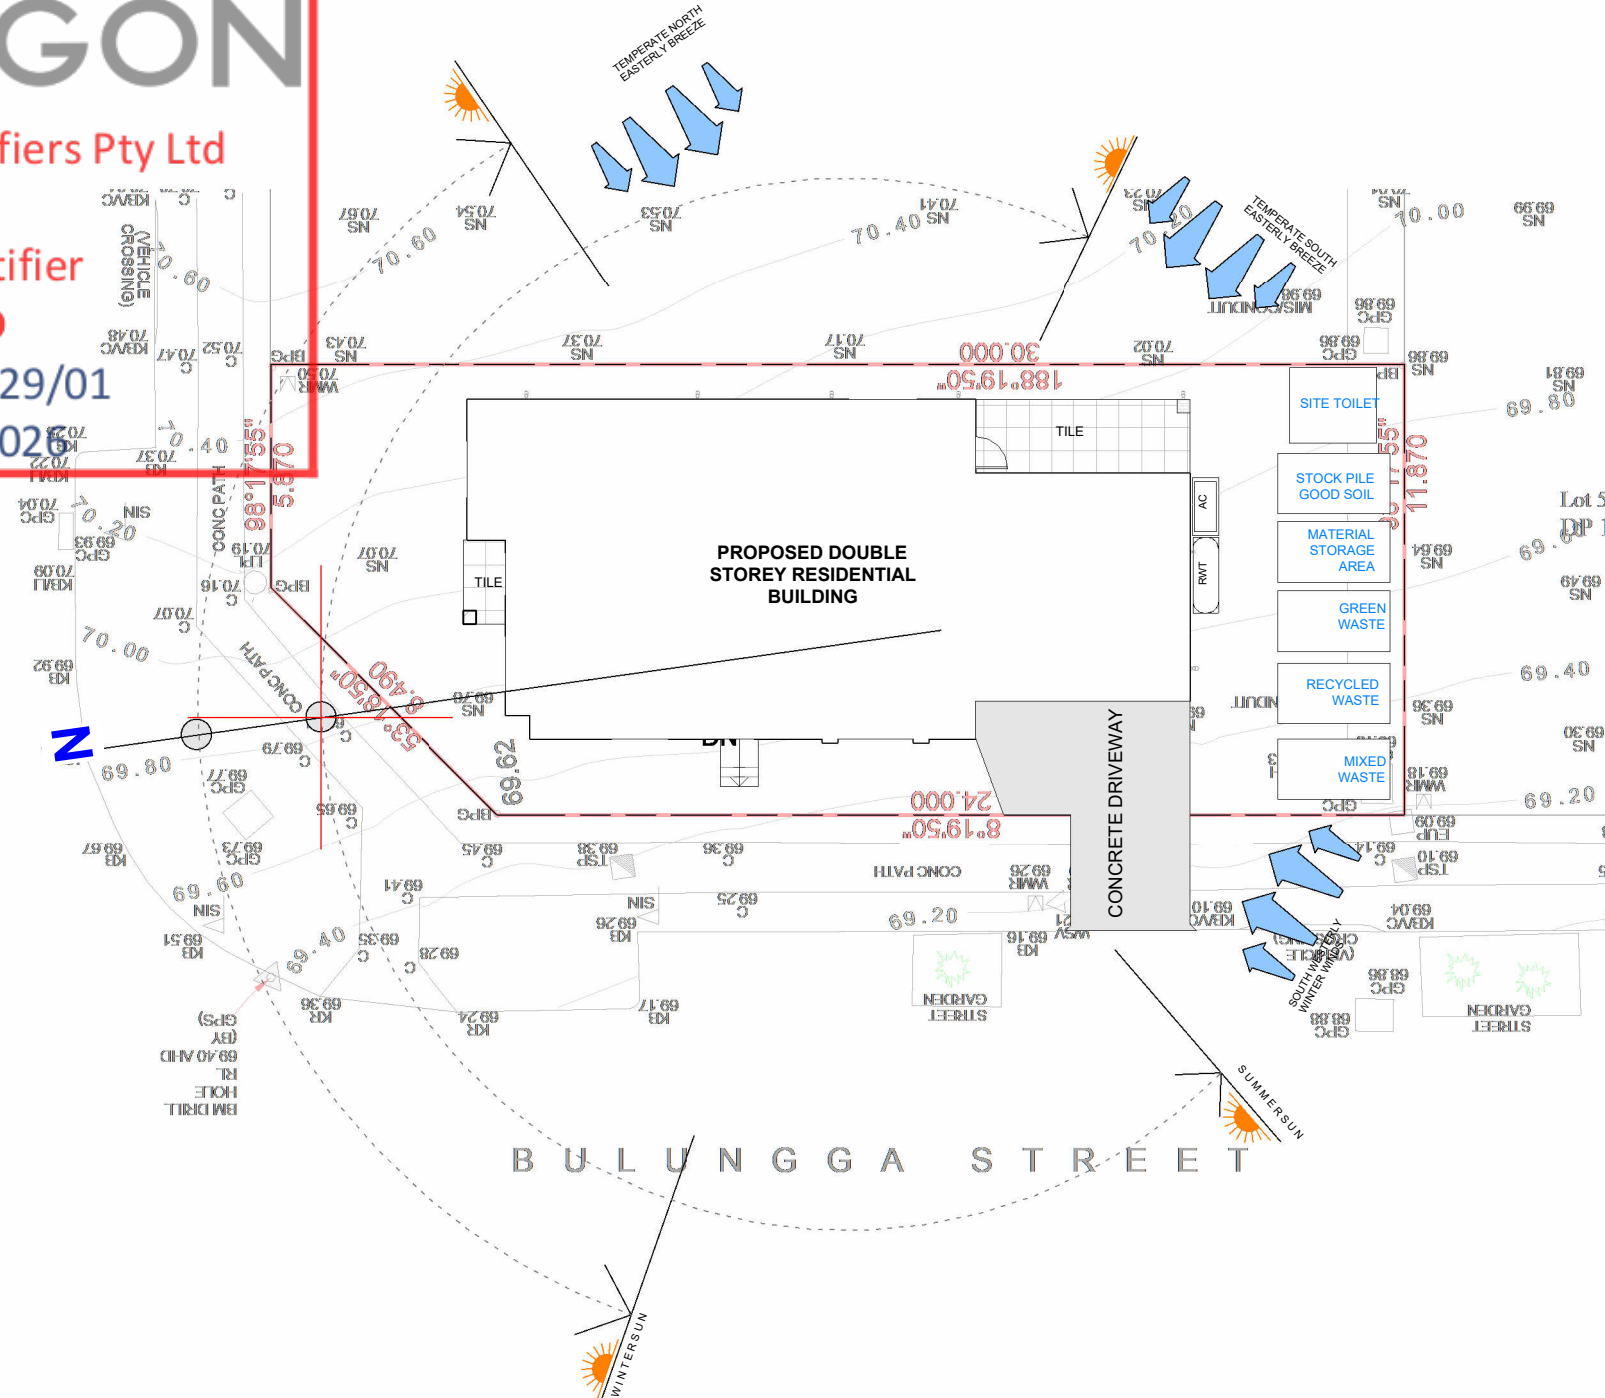

SITE ANALYSIS AND WASTE MANAGEMENT PLAN

1

1 : 200

CC ISSUE


REV	DATE	DESCRIPTION	BY
6	7-09-2026	CC-ISSUE	
5	26-08-2026	DA - Additional Information	
4	6-08-2026	DA ISSUE	
3	29-04-2026	Brick finish to wall and foam render finish to parapet and cladding wall - Ek	



THIS DRAWING IS THE EXCLUSIVE PROPERTY OF THE DEVELOPER & THE REPRODUCTION OF ANY PART WITHOUT THE PRIOR WRITTEN CONSENT OF THE DEVELOPER IS A VIOLATION OF APPLICABLE LAWS. IN NO EVENT SHALL THE DEVELOPER BE HELD LIABLE FOR SPECIAL COLLATERAL, INCIDENTAL OR CONSEQUENTIAL LIABILITY IN CONNECTION WITH THE USE OF THIS DIGITAL DATA ONCE RELEASED FROM THE DEVELOPER'S OFFICE. THIS DRAWING IS TO BE READ & UNDERSTOOD IN CONJUNCTION WITH THE STRUCTURAL, MECHANICAL, ELECTRICAL & / OR ANY OTHER CONSULTANT'S DOCUMENTATION AS MAY BE APPLICABLE TO THE PROJECT PRIOR TO THE START OF ANY WORKS AND FOR ITS DURATION.

PROJECT:
**25 Yabunaru Street
Austral**
Lot 527 in DP1310900 at 25
Yabunaru Street Austral NSW 2179

DRAWING TITLE:
**SITE ANALYSIS AND
WASTE
MANAGEMENT PLAN**

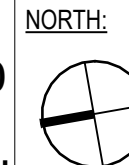

LOT NO: 527	DATE: 8-09-2026	SCALE: As indicated	DRAWING No: CC.04B	REV: 6
DRAWN BY: AS	CHECKED BY: RH			ISSUED BY:
DRAFTED BY: SL	CLIENT NAME: Gokul Prasad Prasai & Sunita Karki Prasai			

Table 3.4.2: Acceptable termite management systems and components

Building element	Termite management system or component options
Concrete slab-on-ground: slab perimeter or external wall perimeter	Slab edge exposure Sheet material Granular material Chemical
Concrete slab-on-ground: penetrations/control joints/area beneath the slab (see Note)	Sheet material Granular material Chemical
Suspended floors	Sheet material Granular material Chemical
Attachments to buildings	Termite management system to the attachment Inspection zone between attachment and building

Paragon Building Certifiers Pty Ltd

RBC00045


Registered Certifier

APPROVED

Reference: 260529/01

Date: 18/09/2026


Figure 11.2.1:

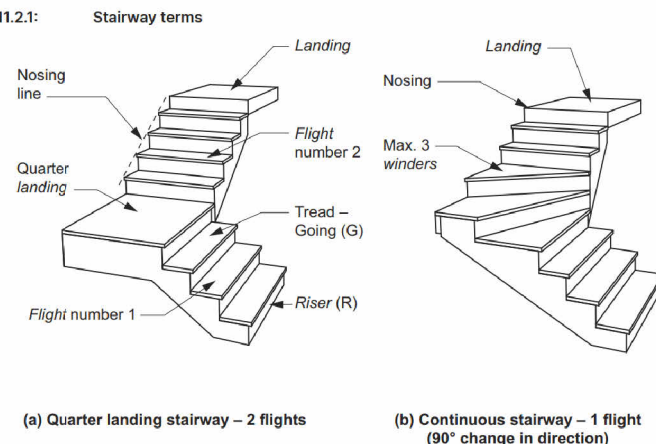

IMPORTANT NOTES:

ALL DIMENSIONS AND NOTES ON ALL PLANS MUST BE CHECKED AND VERIFIED BY BUILDERS AND OWNER PRIOR TO COMMENCEMENT OF ANY BUILDING WORKS. TO CLARIFY AND CONFIRM WITH CONSTRUCTION COMPANY FOR DISCREPANCIES ON ALL DOCUMENTS AND PLANS PROVIDED FOR CONSTRUCTION. ANY WORK INDICATED ON THE PLAN BUT NOT IN THE SPECIFICATION BUT WHICH IS NECESSARY AS PART OF THE CONTRACT, VARIATION TO PLANS, SPECIFICATIONS MAY NOT BE MADE WITHOUT THE WRITTEN CONSENT OF OWNER. IT IS THE RESPONSIBILITY OF THE BUILDER/END USER TO VERIFY PLANS AND SPECIFICATIONS AS TO THEIR ACCURACY AND COMPLY CURRENT BCA AND AUSTRALIAN STANDARDS. WINDOWS TO COMPLY WITH 3.9.3.5 OF THE BCA.

Figure 11.2.2a: Measurement of slope relationship — Plan view — Stair with 2 flights

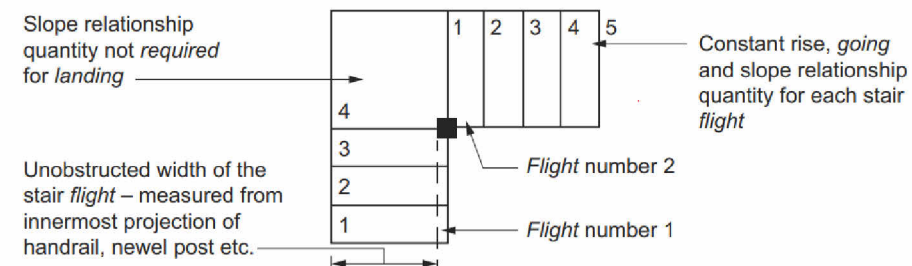

Waterproofing work to be as per Part 10.2 of the ABCB Housing Provisions Standard 2022

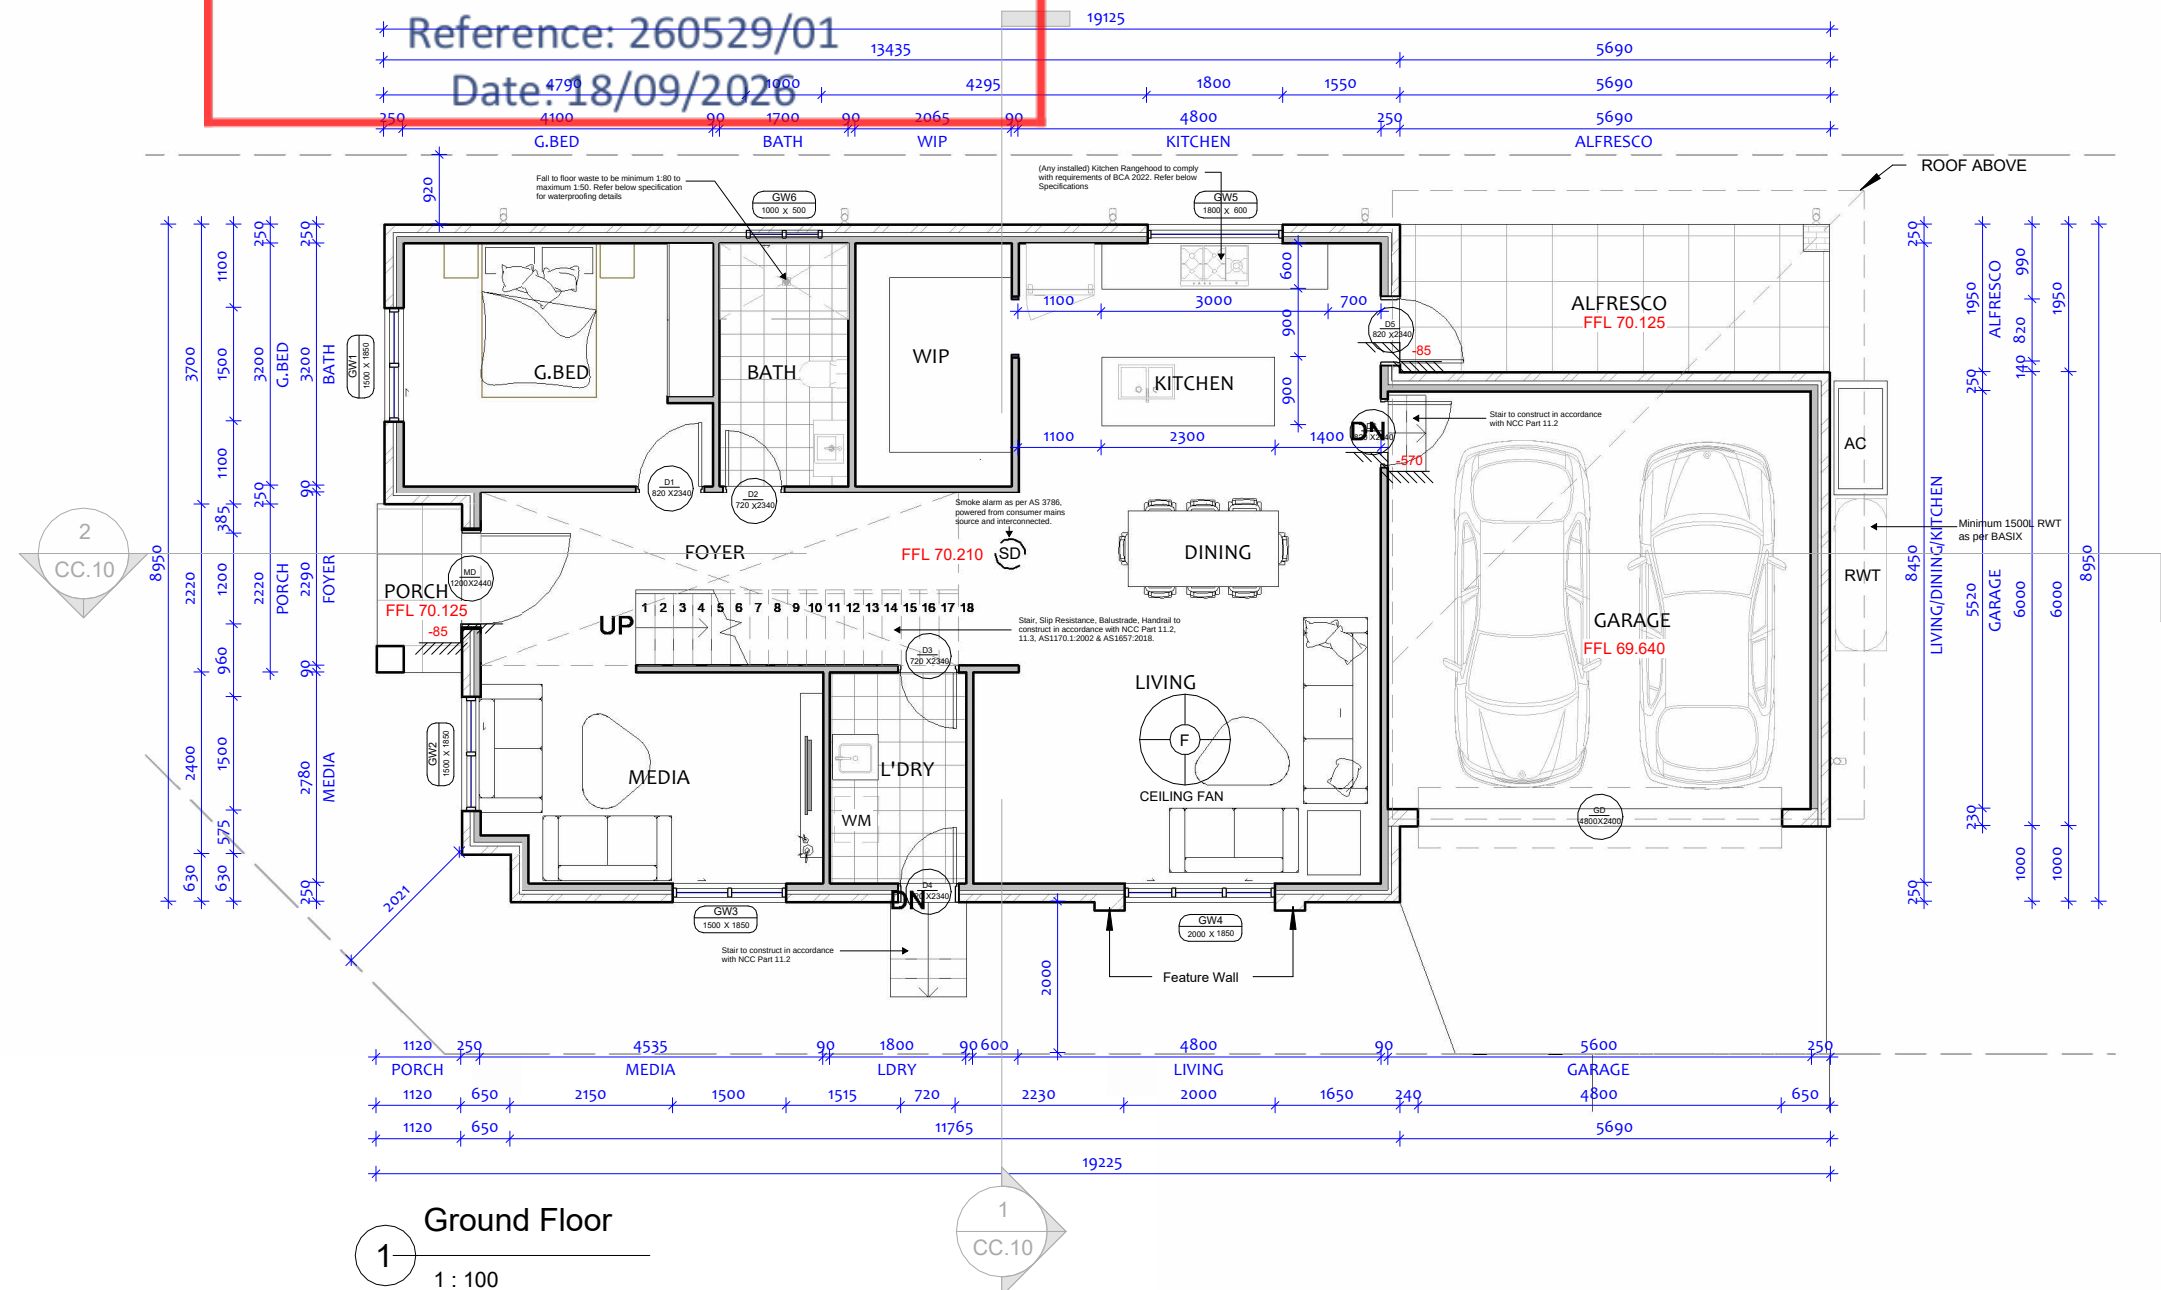


Table 11.2.2b: Riser and going dimensions (mm) — stairways serving non-habitable rooms used infrequently

Riser (R)	Going (G)	Slope relationship (2R+G)
Max	Min	Max
225	130	355

Table 11.2.2a: Riser and going dimensions (mm)

Stair type	Riser (R) (see Figure 11.2.2f)	Going (G) (see Figure 11.2.2f)	Slope relationship (2R+G)
	Max	Min	Max
Stairs (other than spiral)	190	115	355
Spiral	220	140	370

NOTE: PLEASE REFER TO TENDER FOR ALL INCLUSIONS.


REV	DATE	DESCRIPTION	BY
6	7-09-2026	CC-ISSUE	
5	26-08-2026	DA - Additional Information	
4	6-08-2026	DA ISSUE	
3	29-04-2026	Brick finish to wall and foam render finish to parapet and cladding wall - Ek	
1	02-04-2026	Bank Set	

RUBY HOMES

THIS DRAWING IS THE EXCLUSIVE PROPERTY OF THE DEVELOPER & THE REPRODUCTION OF ANY PART WITHOUT THE PRIOR WRITTEN CONSENT OF THE DEVELOPER IS A VIOLATION OF APPLICABLE LAWS. IN NO EVENT SHALL THE DEVELOPER BE HELD LIABLE FOR SPECIAL COLLATERAL, INCIDENTAL OR CONSEQUENTIAL LIABILITY IN CONNECTION WITH THE USE OF THIS DIGITAL DATA ONCE RELEASED FROM THE DEVELOPER'S OFFICE. THIS DRAWING IS TO BE READ & UNDERSTOOD IN CONJUNCTION WITH THE STRUCTURAL, MECHANICAL, ELECTRICAL & / OR ANY OTHER CONSULTANT'S DOCUMENTATION AS MAY BE APPLICABLE TO THE PROJECT PRIOR TO THE START OF ANY WORKS AND FOR ITS DURATION.

PROJECT:
25 Yabunaru Street
Austral
Lot 527 in DP1310900 at 25 Yabunaru Street Austral NSW 2179

DRAWING TITLE:
GROUND FLOOR PLAN

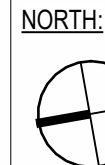

LOT NO:	DATE:	SCALE:	DRAWING No:	REV:
527	8-09-2026	1 : 100	CC.05	6
DRAWN BY:	CHECKED BY:			ISSUED BY:
AS	RH			
DRAFTED BY:	CLIENT NAME:			
SL	Gokul Prasad Prasai & Sunita Karki Prasai			

CC ISSUE



Paragon Building Certifiers Pty Ltd

BBC000045

Registered Certifier


APPROVED

Reference: 260529/01

Date: 18/09/2026

IMPORTANT NOTES:
ALL DIMENSIONS AND NOTES ON ALL PLANS MUST BE CHECKED AND VERIFIED BY BUILDERS AND OWNER PRIOR TO COMMENCEMENT OF ANY BUILDING WORKS. TO CLARIFY AND CONFIRM WITH CONSTRUCTION COMPANY FOR DISCREPANCIES ON ALL DOCUMENTS AND PLANS PROVIDED FOR CONSTRUCTION. ANY WORK INDICATED ON THE PLAN BUT NOT IN THE SPECIFICATION BUT WHICH IS NECESSARY AS PART OF THE CONTRACT, VARIATION TO PLANS, SPECIFICATIONS MAY NOT BE MADE WITHOUT THE WRITTEN CONSENT OF OWNER. IT IS THE RESPONSIBILITY OF THE BUILDER/END USER TO VERIFY PLANS AND SPECIFICATIONS AS TO THEIR ACCURACY AND COMPLY CURRENT BCA AND AUSTRALIAN STANDARDS. WINDOWS TO COMPLY WITH 3.9.3.5 OF THE BCA.

Waterproofing work to be as per Part 10.2 of the ABCB Housing Provisions Standard 2022

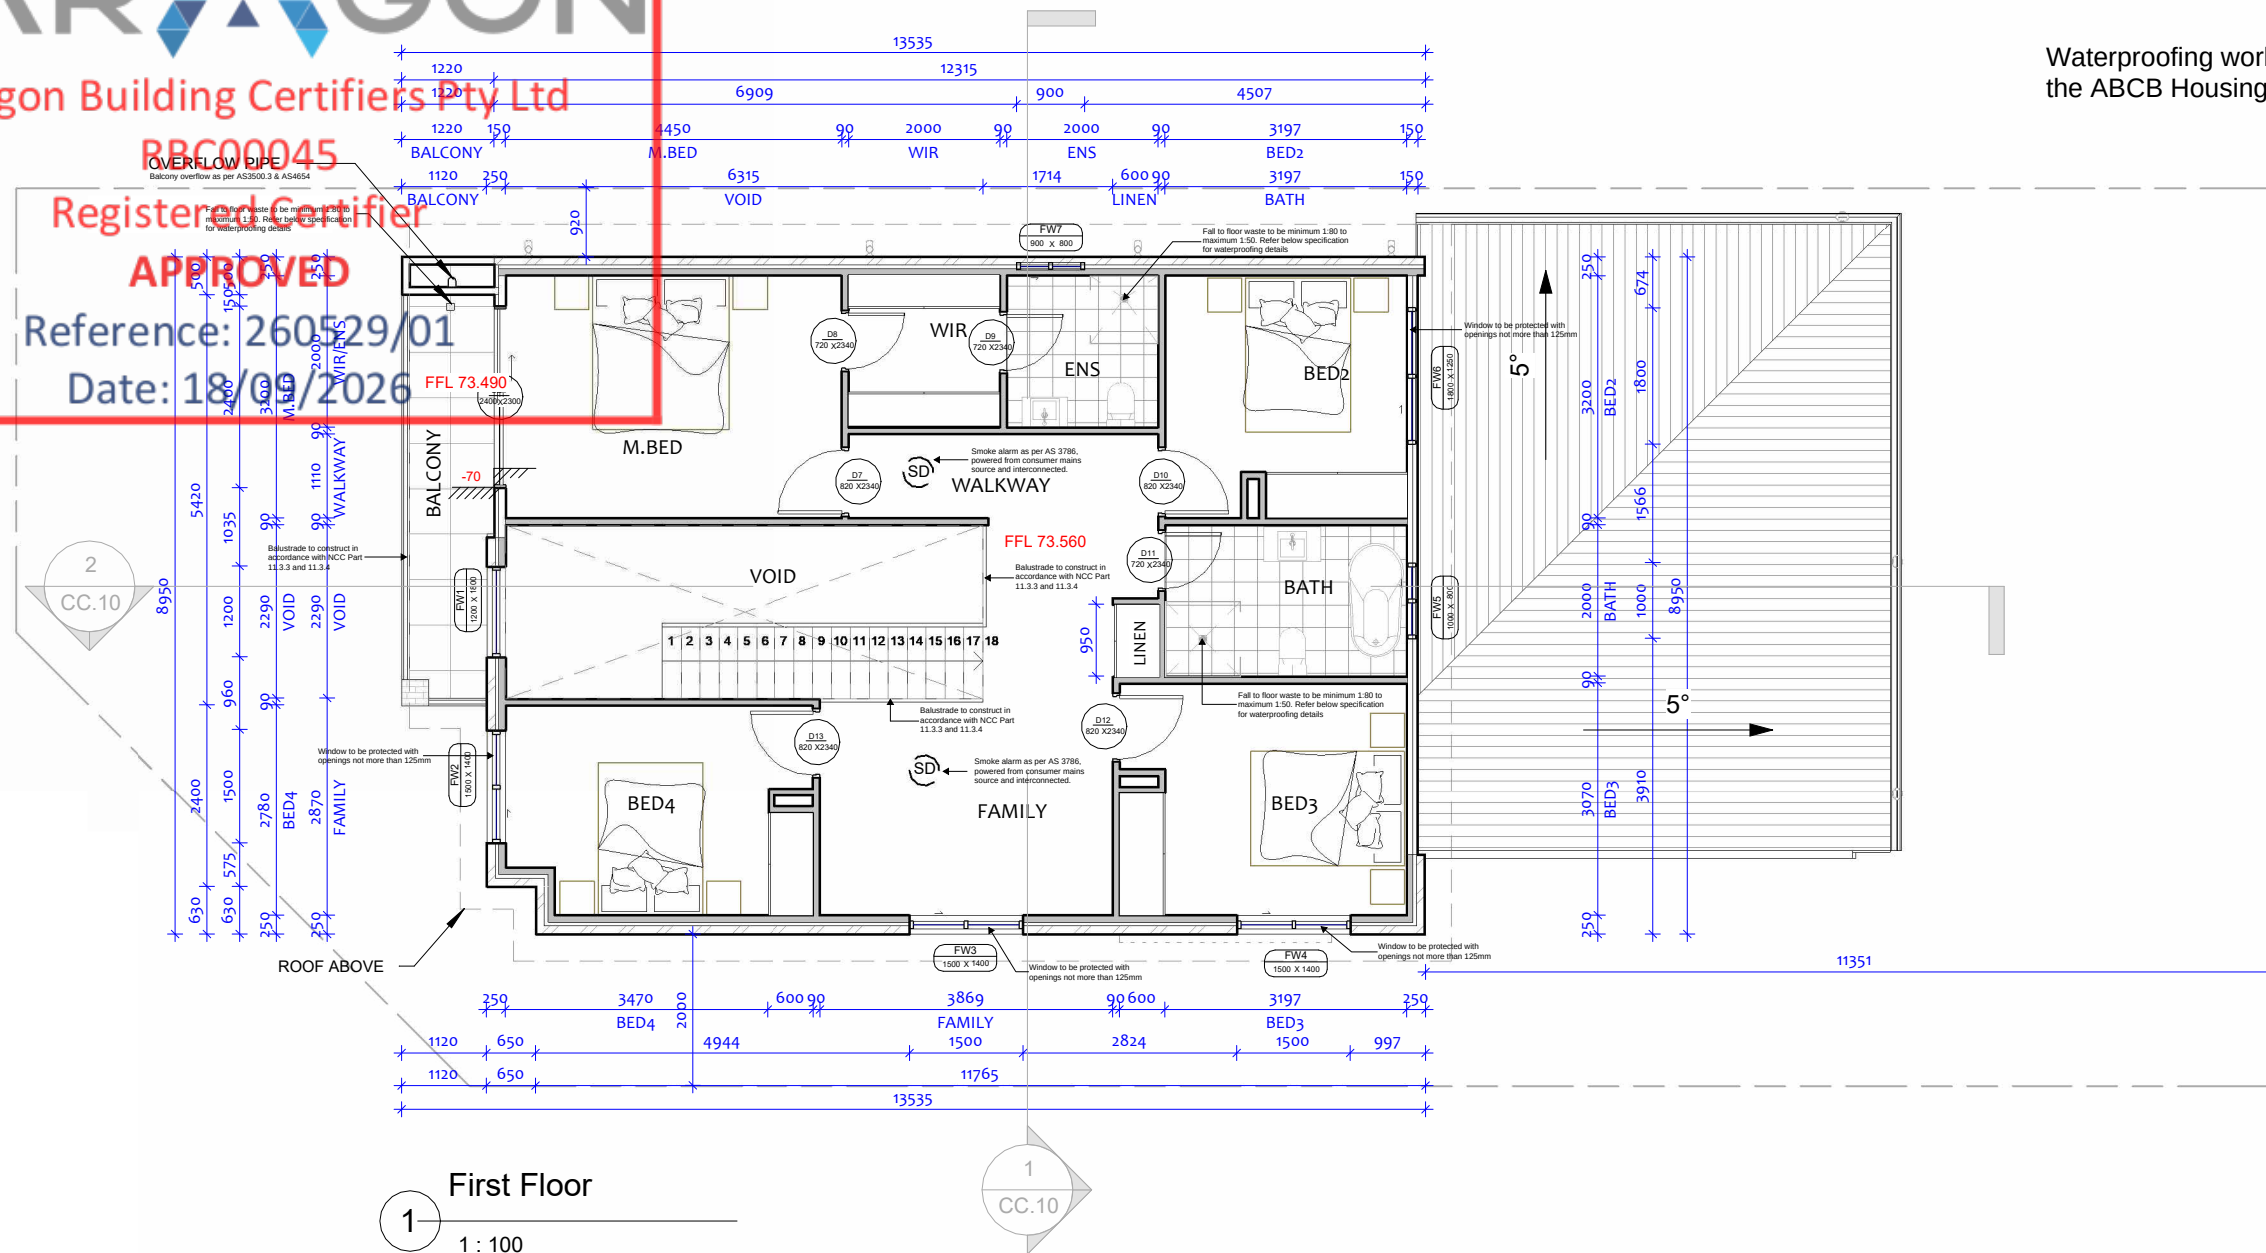

NOTE: PLEASE REFER TO TENDER FOR ALL INCLUSIONS.


REV	DATE	DESCRIPTION	BY
6	7-09-2026	CC-ISSUE	
5	26-08-2026	DA - Additional Information	
4	6-08-2026	DA ISSUE	
3	29-04-2026	Brick finish to wall and foam render finish to parapet and cladding wall - Ek	
2	3-04-2026	Brick column added at balcony - Ek	
1	02-04-2026	Bank Set	



THIS DRAWING IS THE EXCLUSIVE PROPERTY OF THE DEVELOPER & THE REPRODUCTION OF ANY PART WITHOUT THE PRIOR WRITTEN CONSENT OF THE DEVELOPER IS A VIOLATION OF APPLICABLE LAWS. IN NO EVENT SHALL THE DEVELOPER BE HELD LIABLE FOR SPECIAL COLLATERAL, INCIDENTAL OR CONSEQUENTIAL LIABILITY IN CONNECTION WITH THE USE OF THIS DIGITAL DATA ONCE RELEASED FROM THE DEVELOPER'S OFFICE. THIS DRAWING IS TO BE READ & UNDERSTOOD IN CONJUNCTION WITH THE STRUCTURAL, MECHANICAL, ELECTRICAL & / OR ANY OTHER CONSULTANT'S DOCUMENTATION AS MAY BE APPLICABLE TO THE PROJECT PRIOR TO THE START OF ANY WORKS AND FOR ITS DURATION.

PROJECT:
25 Yabunaru Street
Austral
Lot 527 in DP1310900 at 25 Yabunaru Street Austral NSW 2179



DRAWING TITLE:
FIRST FLOOR LEVEL

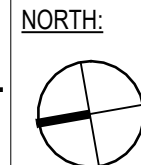

CC ISSUE			
LOT NO:	DATE:	SCALE:	DRAWING No: REV:
527	8-09-2026	1 : 100	CC.06 6
DRAWN BY:	CHECKED BY:	ISSUED BY:	
AS	RH		
DRAFTED BY:	CLIENT NAME:		
SL	Gokul Prasad Prasai & Sunita Karki Prasai		

IMPORTANT NOTES:
ALL DIMENSIONS AND NOTES ON ALL PLANS MUST BE CHECKED AND VERIFIED BY BUILDERS AND OWNER PRIOR TO COMMENCEMENT OF ANY BUILDING WORKS. TO CLARIFY AND CONFIRM WITH CONSTRUCTION COMPANY FOR DISCREPANCIES ON ALL DOCUMENTS AND PLANS PROVIDED FOR CONSTRUCTION. ANY WORK INDICATED ON THE PLAN BUT NOT IN THE SPECIFICATION BUT WHICH IS NECESSARY AS PART OF THE CONTRACT, VARIATION TO PLANS, SPECIFICATIONS MAY NOT BE MADE WITHOUT THE WRITTEN CONSENT OF OWNER. IT IS THE RESPONSIBILITY OF THE BUILDER/END USER TO VERIFY PLANS AND SPECIFICATIONS AS TO THEIR ACCURACY AND COMPLY CURRENT BCA AND AUSTRALIAN STANDARDS. WINDOWS TO COMPLY WITH 3.9.3.5 OF THE BCA.

Minimum pitch requirements for metal roofing profiles

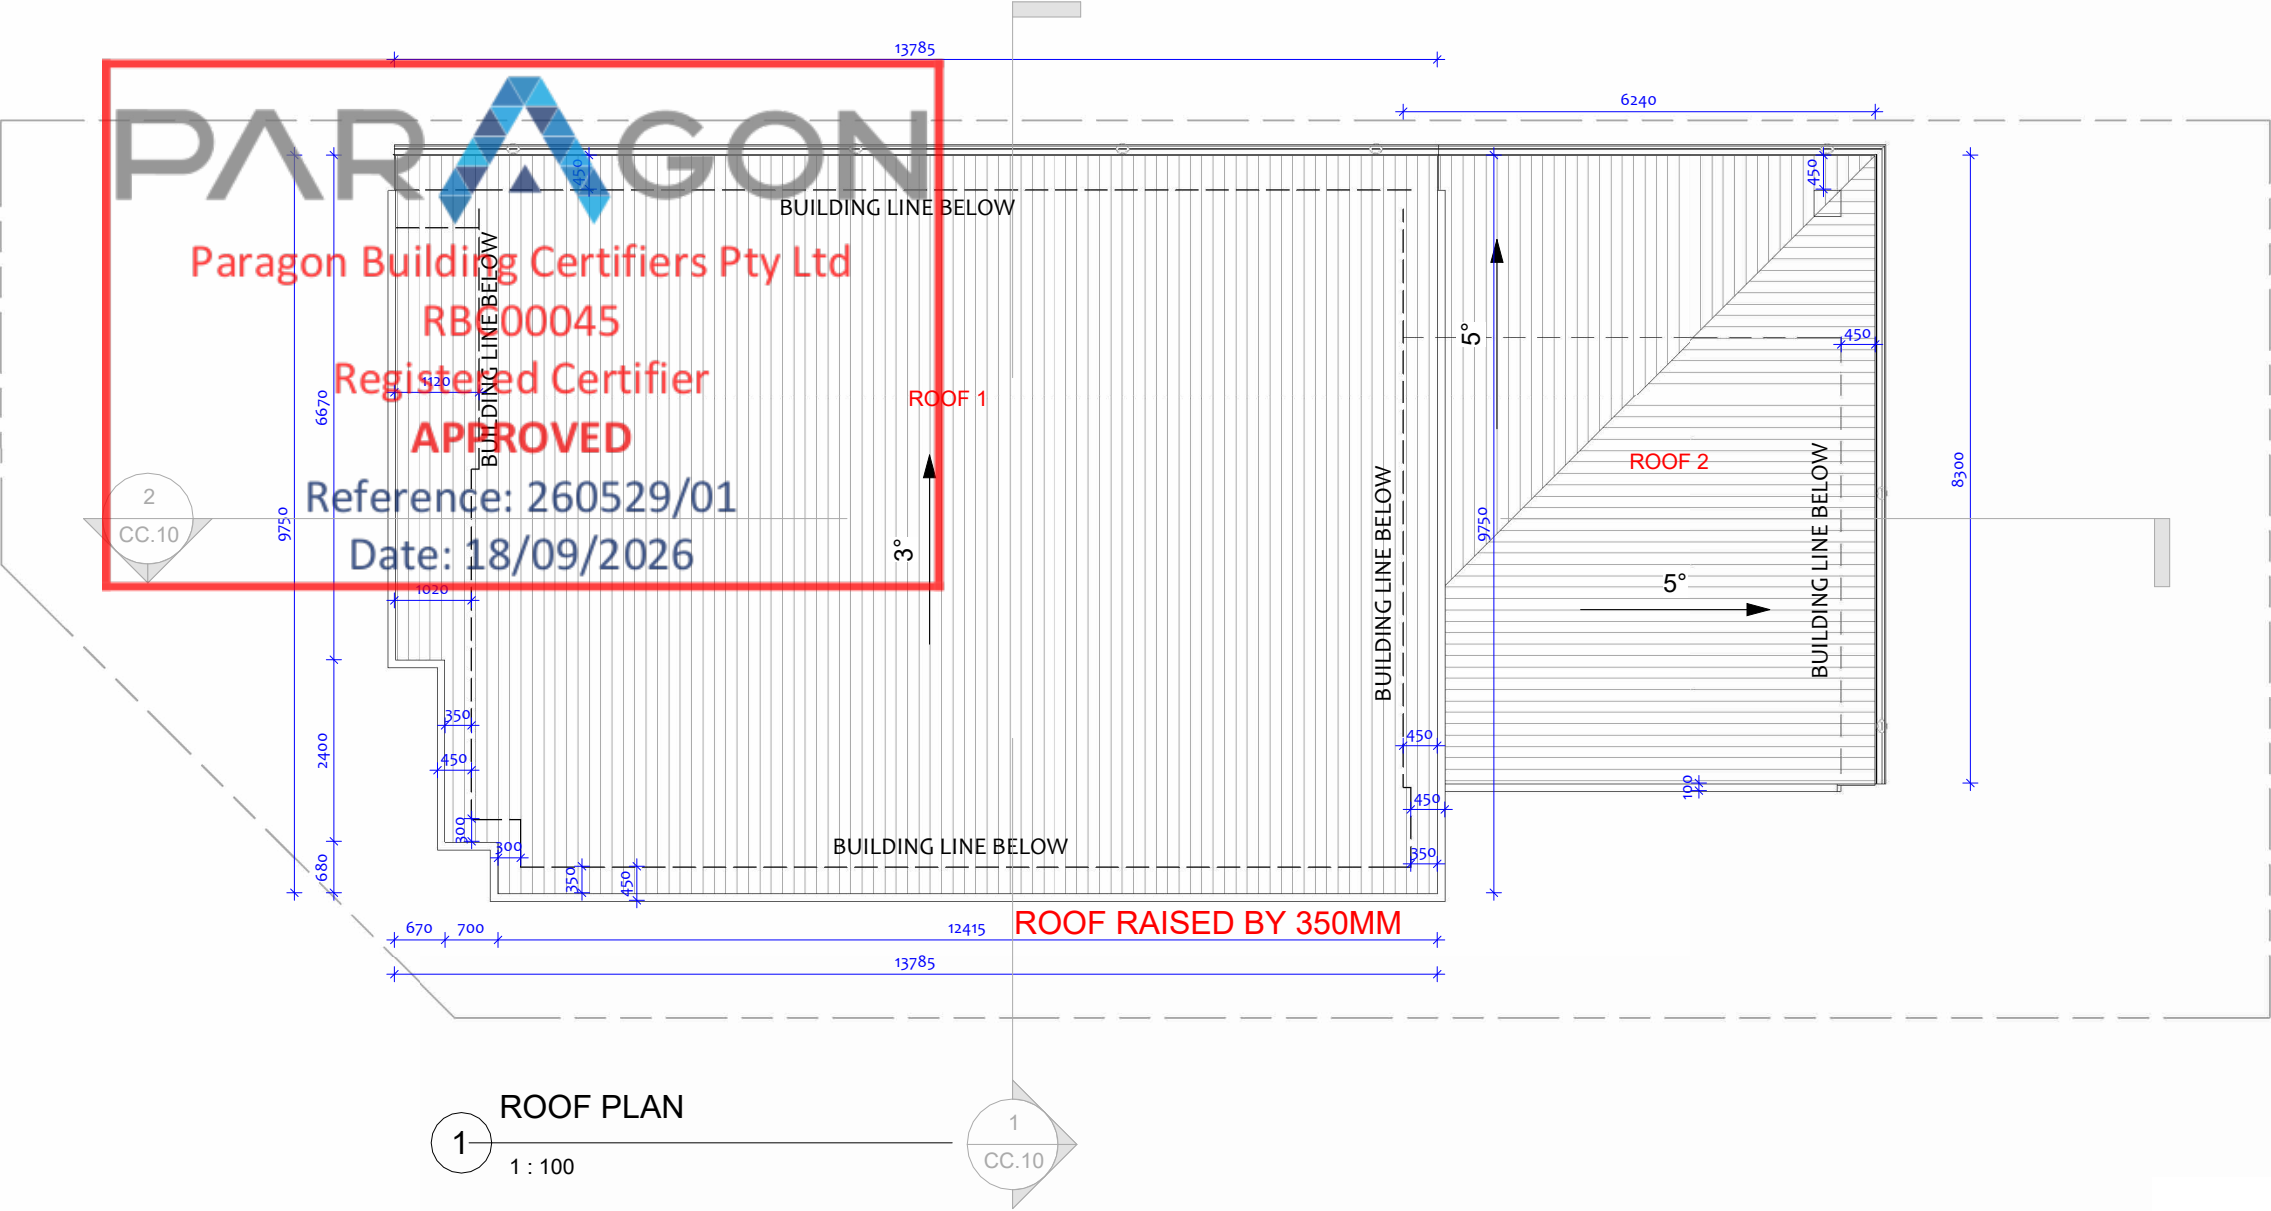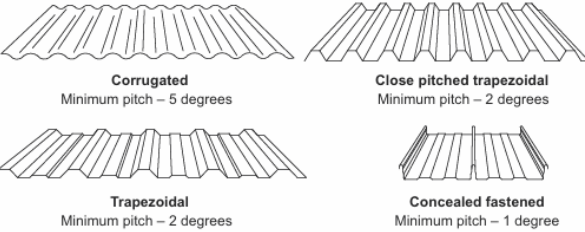

VENTILATION OF ROOF SPACES

ROOF SPACE AS PER 10.8.3 1(a) & 1(b)

(i) VENTILATED TO OUTDOOR AIR THROUGH EVENLY DISTRIBUTED OPENINGS IN ACCORDANCE WITH TABLE 10.8.3;

TABLE 10.8.3: ROOF SPACE VENTILATION REQUIREMENTS

ROOF PITCH	VENTILATION OPENINGS
< 10°	25,000 MM2/M PROVIDED AT EACH OF TWO OPPOSING ENDS
≥ 10° AND < 15°	25,000 MM2/M PROVIDED AT THE EAVES AND 5,000 MM2/M AT HIGH LEVEL
≥ 15° AND < 75°	7,000 MM2/M PROVIDED AT THE EAVES AND 5,000 MM2/M AT HIGH LEVEL, PLUS AN ADDITIONAL 18,000 MM2/M AT THE EAVES IF THE ROOF HAS A CATHEDRAL CEILING




Roof Schedule			
Mark	Base Level	Area	Comments
ROOF2	First Floor	52 m²	COLORBOND
ROOF 1	CEILING LEVEL	132 m²	COLORBOND
Grand total: 2		184 m²	

REV	DATE	DESCRIPTION	BY
6	7-09-2026	CC-ISSUE	
5	26-08-2026	DA - Additional Information	
4	6-08-2026	DA ISSUE	
3	29-04-2026	Brick finish to wall and foam render finish to parapet and cladding wall - Ek	


THIS DRAWING IS THE EXCLUSIVE PROPERTY OF THE DEVELOPER & THE REPRODUCTION OF ANY PART WITHOUT THE PRIOR WRITTEN CONSENT OF THE DEVELOPER IS A VIOLATION OF APPLICABLE LAWS. IN NO EVENT SHALL THE DEVELOPER BE HELD LIABLE FOR SPECIAL COLLATERAL, INCIDENTAL OR CONSEQUENTIAL LIABILITY IN CONNECTION WITH THE USE OF THIS DIGITAL DATA ONCE RELEASED FROM THE DEVELOPER'S OFFICE. THIS DRAWING IS TO BE READ & UNDERSTOOD IN CONJUNCTION WITH THE STRUCTURAL, MECHANICAL, ELECTRICAL & / OR ANY OTHER CONSULTANT'S DOCUMENTATION AS MAY BE APPLICABLE TO THE PROJECT PRIOR TO THE START OF ANY WORKS AND FOR ITS DURATION.

PROJECT:
25 Yabunaru Street
Austral
Lot 527 in DP1310900 at 25 Yabunaru Street Austral NSW 2179

DRAWING TITLE:
ROOF PLAN

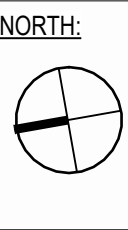


LOT NO: 527	DATE: 8-09-2026	SCALE: 1 : 100	DRAWING No: CC.07	REV: 6
DRAWN BY: AS	CHECKED BY: RH			ISSUED BY:
DRAFTED BY: SL	CLIENT NAME: Gokul Prasad Prasai & Sunita Karki Prasai			

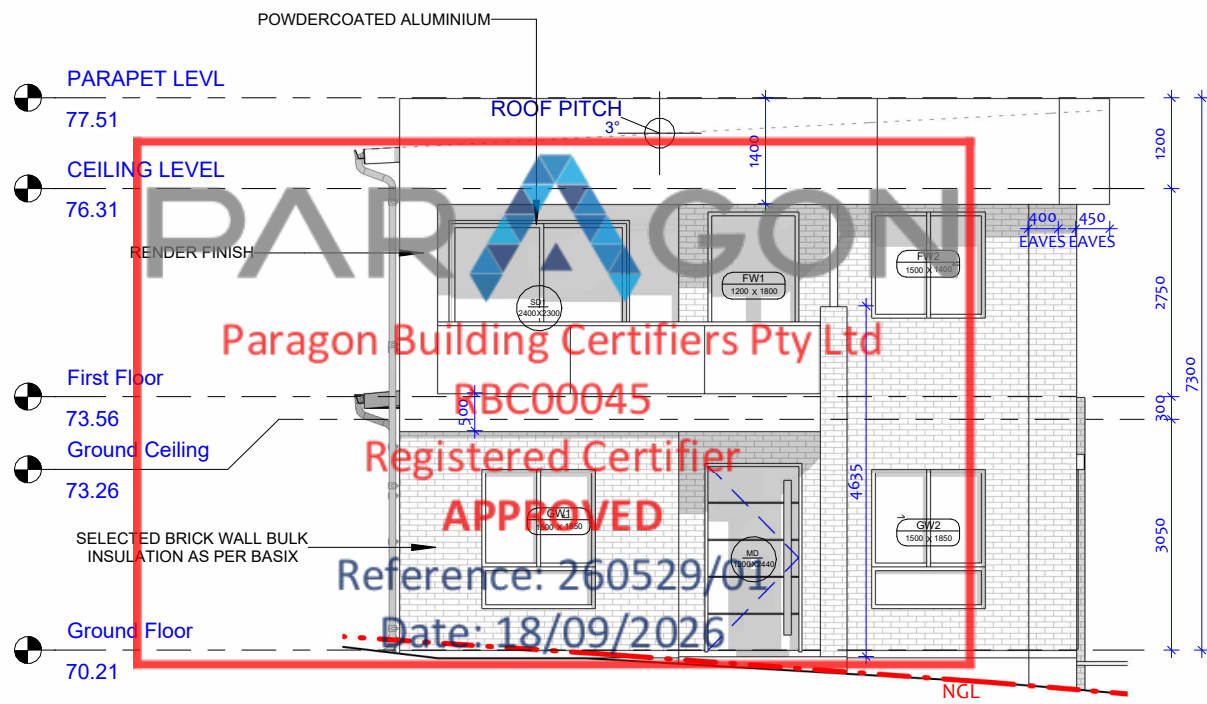

NORTH ELEVATION

1
1 : 100

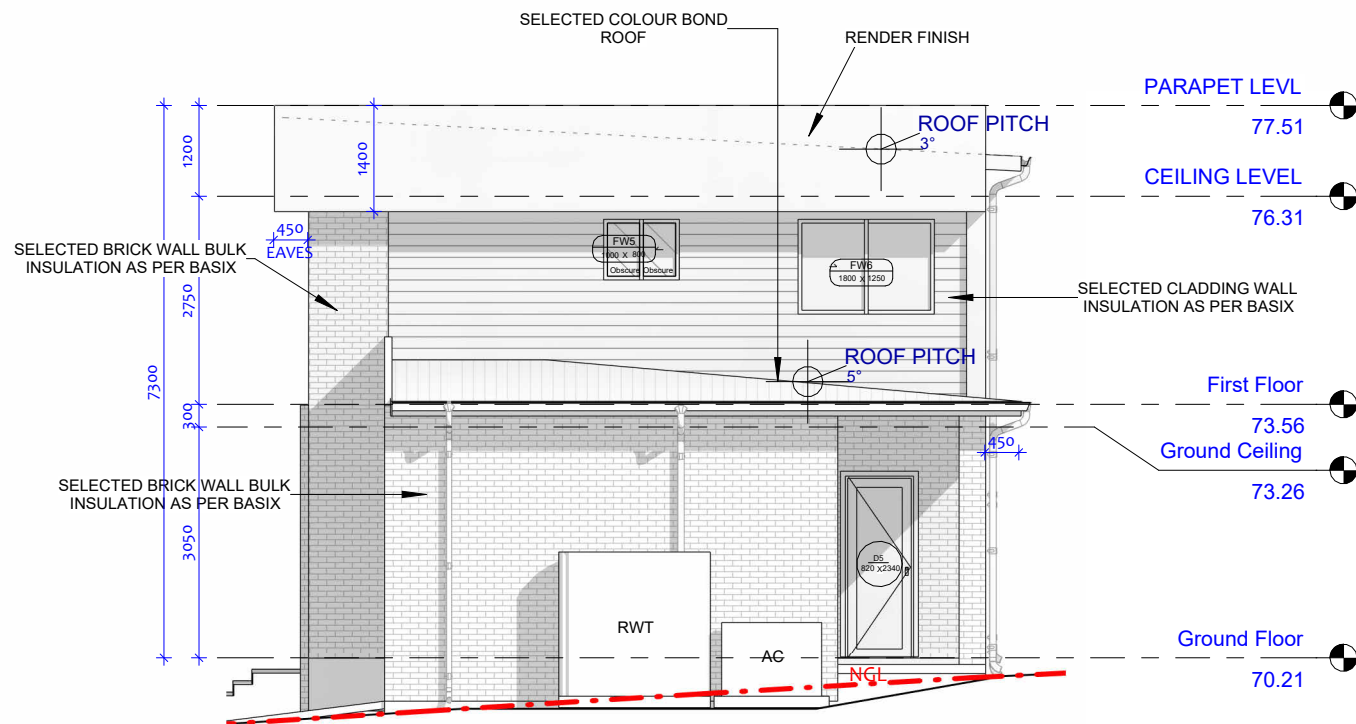

SOUTH ELEVATION

2
1 : 100

Window Schedule 1

Mark	Width	Height	Sill Height	Head Height	Description
Ground Floor					
GW1	1500	1850	550	2400	SLIDING
GW2	1500	1850	550	2400	SLIDING
GW3	1500	1850	550	2400	SLIDING
GW4	2000	1850	550	2400	SLIDING
GW5	1800	600	950	1550	FIXED
GW6	1000	500	1900	2400	SLIDING

Ground Floor: 6

First Floor

FW1	1200	1800	650	2450	FIXED
FW2	1500	1400	1050	2450	SLIDING
FW3	1500	1400	1050	2450	SLIDING
FW4	1500	1400	1050	2450	SLIDING
FW5	1000	800	1650	2450	SLIDING
FW6	1800	1250	1200	2450	SLIDING
FW7	900	800	1650	2450	SLIDING

First Floor: 7

Door Schedule 1

Mark	Width	Height	Count	Description
------	-------	--------	-------	-------------

Garage level

GD	4800	2400	1	GARAGE DOOR
----	------	------	---	-------------

Garage level: 1

Ground Floor

D1	820	2340	1	FLUSH DOOR
D2	720	2340	1	FLUSH DOOR
D3	720	2340	1	FLUSH DOOR
D4	720	2340	1	FLUSH DOOR
D5	820	2340	1	GLAZED DOOR
D6	820	2340	1	FLUSH DOOR
MD	1200	2440	1	SOLID CORE DOOR

Ground Floor: 7

First Floor

D7	820	2340	1	FLUSH DOOR
D8	720	2340	1	FLUSH DOOR
D9	720	2340	1	FLUSH DOOR
D10	820	2340	1	FLUSH DOOR
D11	720	2340	1	FLUSH DOOR
D12	820	2340	1	FLUSH DOOR
D13	820	2340	1	FLUSH DOOR
SD1	2400	2300	1	SLIDING DOOR

First Floor: 8

CC ISSUE

REV	DATE	DESCRIPTION	BY
6	7-09-2026	CC-ISSUE	
5	26-08-2026	DA - Additional Information	
4	6-08-2026	DA ISSUE	
3	29-04-2026	Brick finish to wall and foam render finish to parapet and cladding wall - Ek	
1	02-04-2026	Bank Set	



RUBY
HOMES


THIS DRAWING IS THE EXCLUSIVE PROPERTY OF THE DEVELOPER & THE REPRODUCTION OF ANY PART WITHOUT THE PRIOR WRITTEN CONSENT OF THE DEVELOPER IS A VIOLATION OF APPLICABLE LAWS. IN NO EVENT SHALL THE DEVELOPER BE HELD LIABLE FOR SPECIAL COLLATERAL, INCIDENTAL OR CONSEQUENTIAL LIABILITY IN CONNECTION WITH THE USE OF THIS DIGITAL DATA ONCE RELEASED FROM THE DEVELOPER'S OFFICE. THIS DRAWING IS TO BE READ & UNDERSTOOD IN CONJUNCTION WITH THE STRUCTURAL, MECHANICAL, ELECTRICAL & / OR ANY OTHER CONSULTANT'S DOCUMENTATION AS MAY BE APPLICABLE TO THE PROJECT PRIOR TO THE START OF ANY WORKS AND FOR ITS DURATION.

PROJECT:
**25 Yabunaru Street
Austral**
Lot 527 in DP1310900 at 25
Yabunaru Street Austral NSW 2179

DRAWING TITLE:
ELEVATION 01


NORTH:

LOT NO: 527	DATE: 8-09-2026	SCALE: 1 : 100	DRAWING No: CC.08	REV: 6
DRAWN BY: AS	CHECKED BY: RH			ISSUED BY:
DRAFTED BY: SL	CLIENT NAME: Gokul Prasad Prasai & Sunita Karki Prasai			

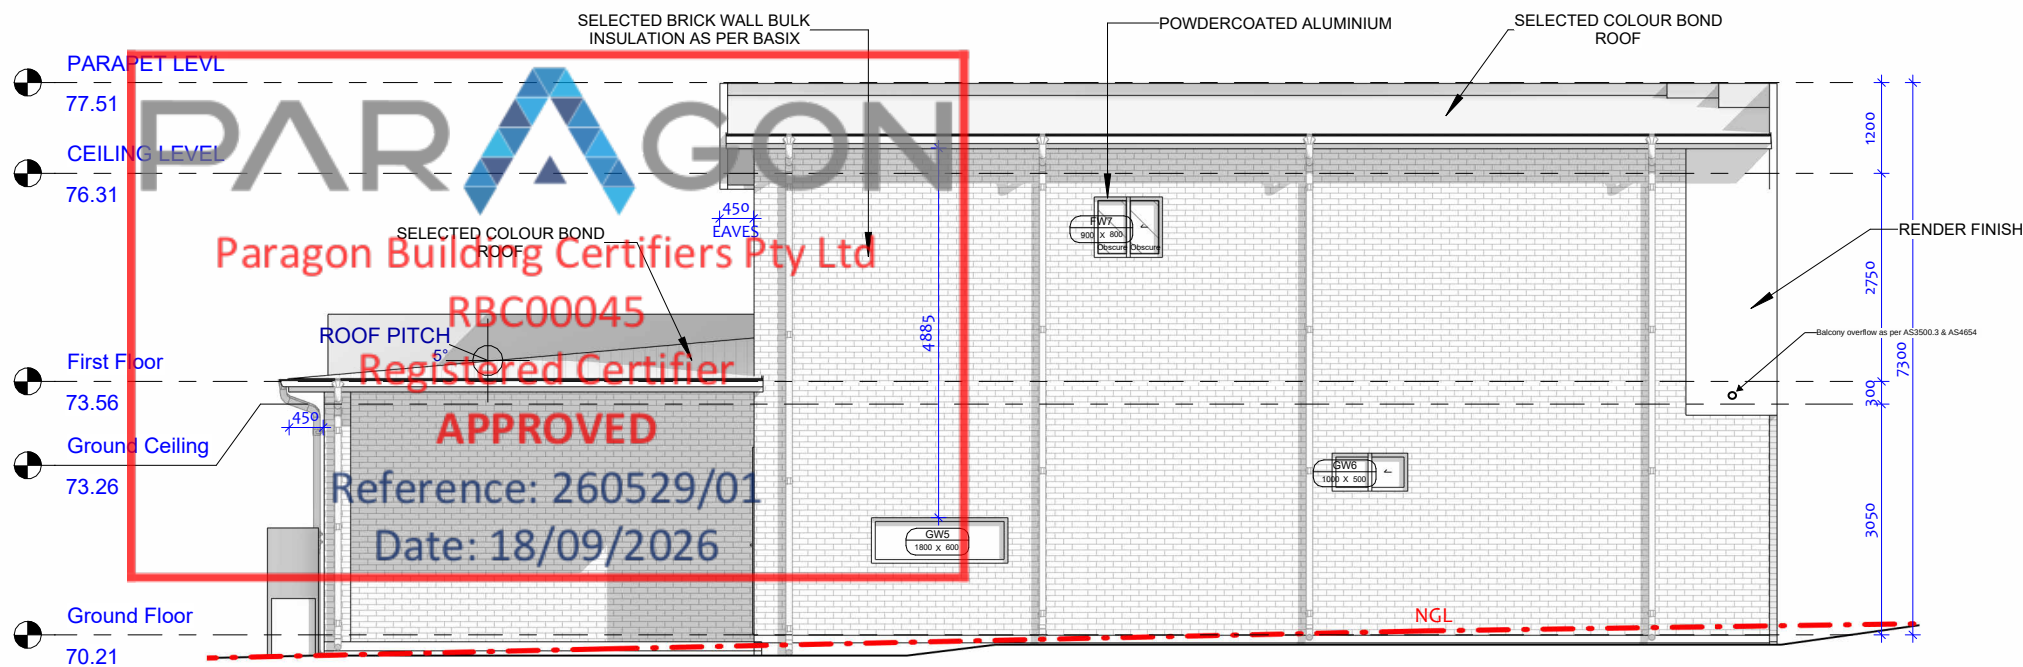

EAST ELEVATION

1
1 : 100

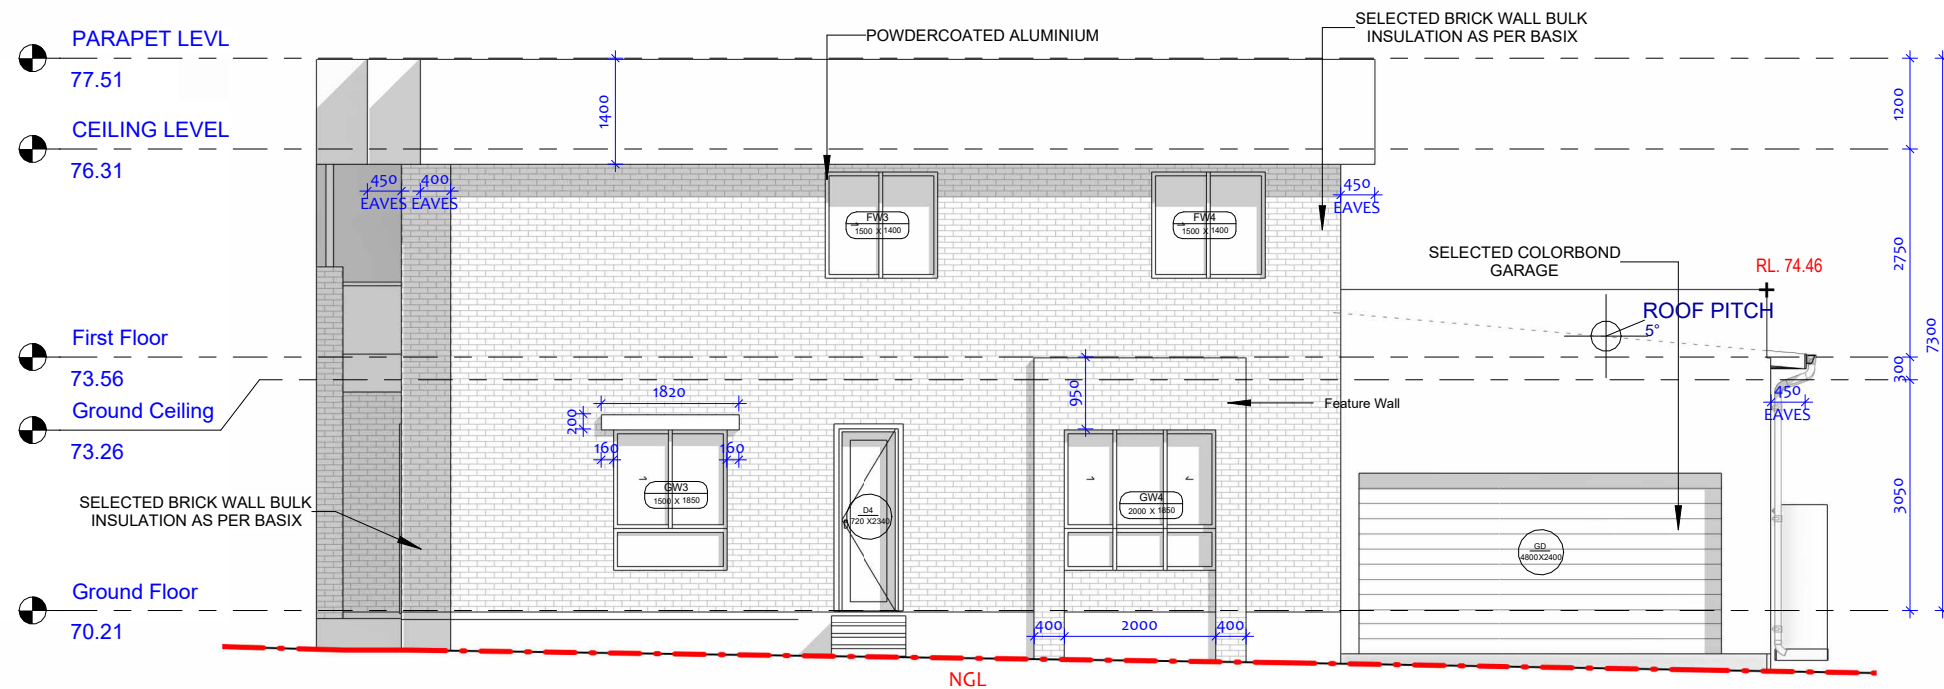

WEST ELEVATION

2
1 : 100

REV	DATE	DESCRIPTION	BY
6	7-09-2026	CC-ISSUE	
5	26-08-2026	DA - Additional Information	
4	6-08-2026	DA ISSUE	
3	29-04-2026	Brick finish to wall and foam render finish to parapet and cladding wall - Ek	
1	02-04-2026	Bank Set	



 THIS DRAWING IS THE EXCLUSIVE PROPERTY OF THE DEVELOPER & THE REPRODUCTION OF ANY PART WITHOUT THE PRIOR WRITTEN CONSENT OF THE DEVELOPER IS A VIOLATION OF APPLICABLE LAWS. IN NO EVENT SHALL THE DEVELOPER BE HELD LIABLE FOR SPECIAL COLLATERAL, INCIDENTAL OR CONSEQUENTIAL LIABILITY IN CONNECTION WITH THE USE OF THIS DIGITAL DATA ONCE RELEASED FROM THE DEVELOPER'S OFFICE. THIS DRAWING IS TO BE READ & UNDERSTOOD IN CONJUNCTION WITH THE STRUCTURAL, MECHANICAL, ELECTRICAL & / OR ANY OTHER CONSULTANT'S DOCUMENTATION AS MAY BE APPLICABLE TO THE PROJECT PRIOR TO THE START OF ANY WORKS AND FOR ITS DURATION.


PROJECT:
25 Yabunaru Street
Austral
 Lot 527 in DP1310900 at 25
 Yabunaru Street Austral NSW 2179

DRAWING TITLE:
ELEVATION 02


NORTH:

LOT NO:	DATE:	SCALE:	DRAWING No:	REV:
527	8-09-2026	1 : 100	CC.09	6
DRAWN BY:	CHECKED BY:			ISSUED BY:
AS	RH			
DRAFTED BY:	CLIENT NAME:			
SL	Gokul Prasad Prasai & Sunita Karki Prasai			

CC ISSUE

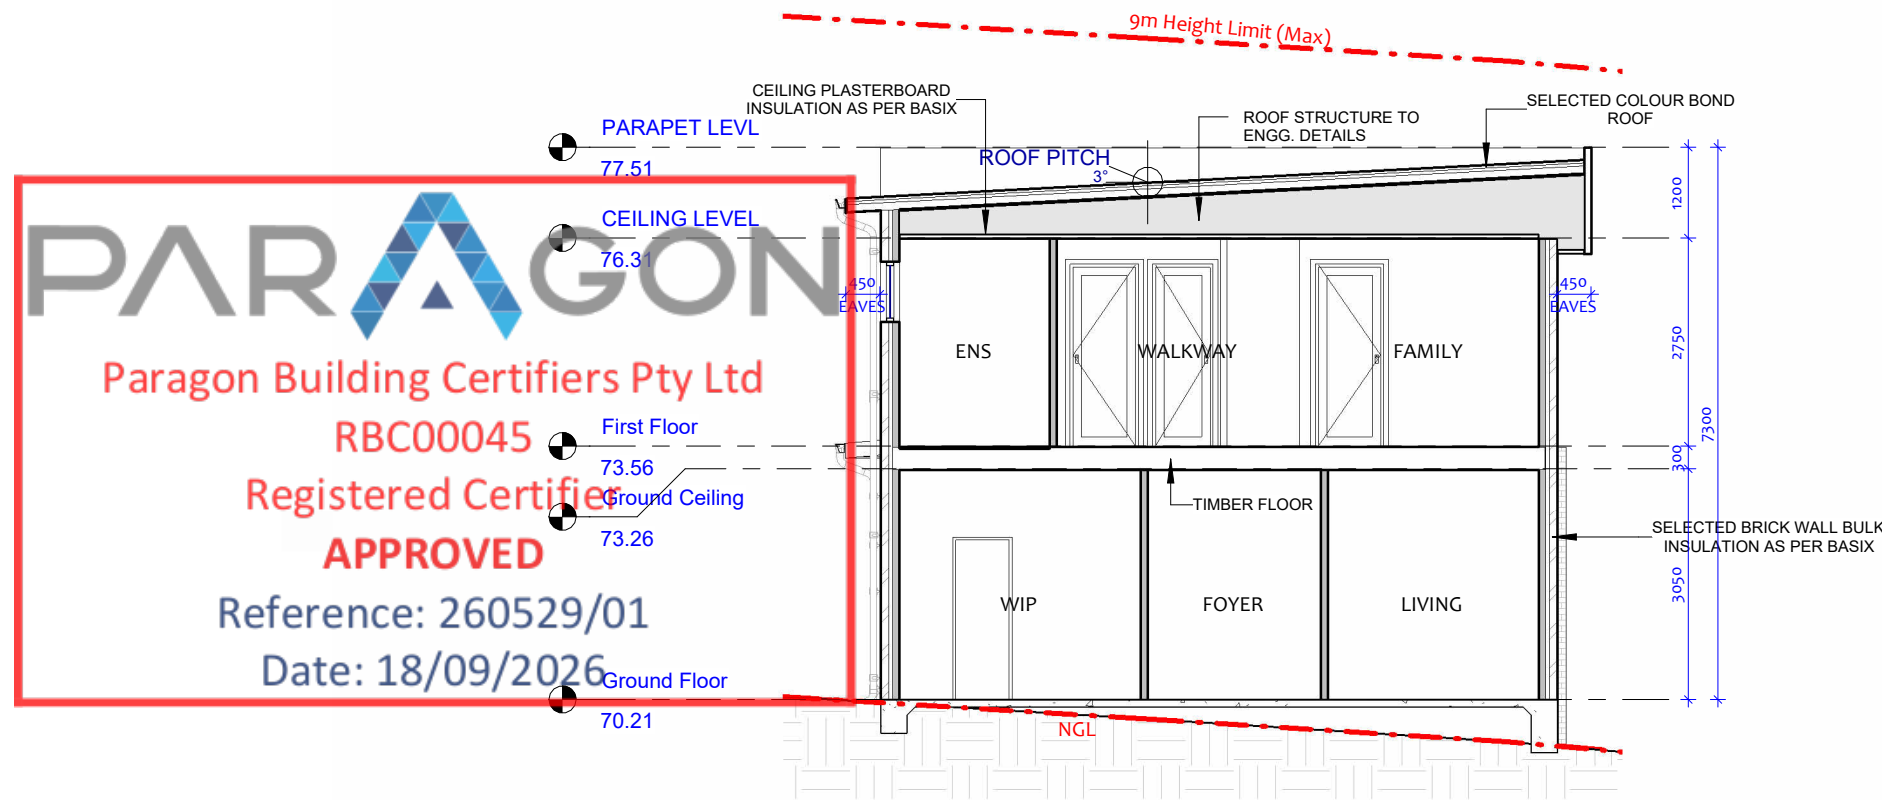

1 CROSS SECTION
1 : 100

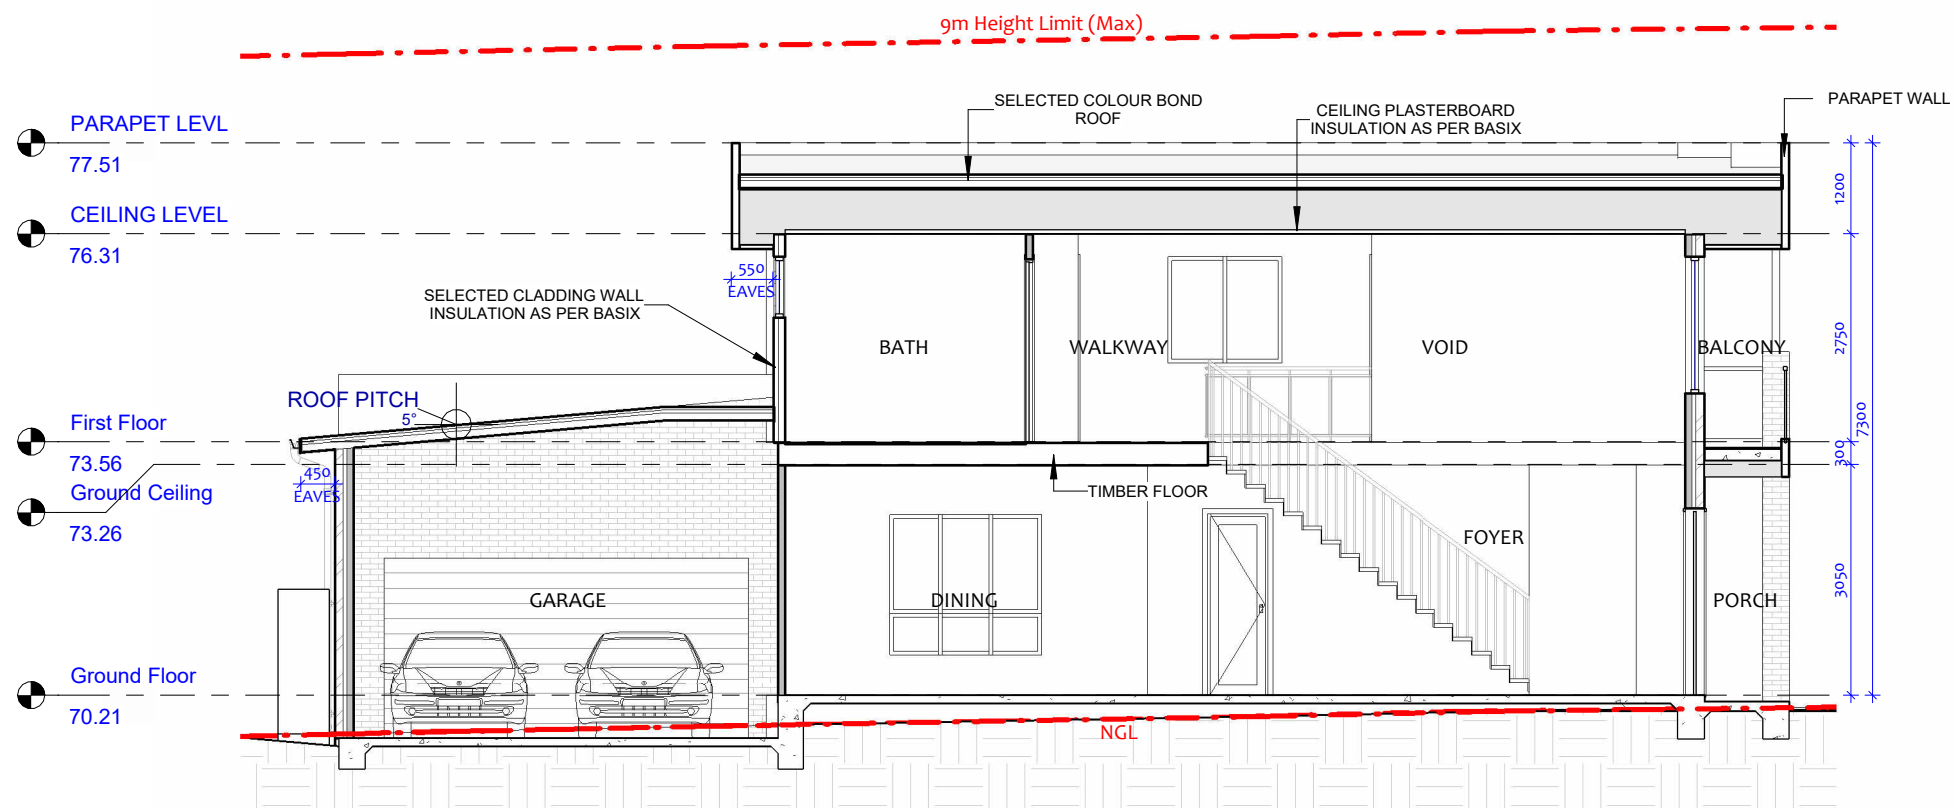

2 LONGITUDINAL SECTION
1 : 100

REV	DATE	DESCRIPTION	BY
6	7-09-2026	CC-ISSUE	
5	26-08-2026	DA - Additional Information	
4	6-08-2026	DA ISSUE	
3	29-04-2026	Brick finish to wall and foam render finish to parapet and cladding wall - Ek	


THIS DRAWING IS THE EXCLUSIVE PROPERTY OF THE DEVELOPER & THE REPRODUCTION OF ANY PART WITHOUT THE PRIOR WRITTEN CONSENT OF THE DEVELOPER IS A VIOLATION OF APPLICABLE LAWS. IN NO EVENT SHALL THE DEVELOPER BE HELD LIABLE FOR SPECIAL COLLATERAL, INCIDENTAL OR CONSEQUENTIAL LIABILITY IN CONNECTION WITH THE USE OF THIS DIGITAL DATA ONCE RELEASED FROM THE DEVELOPER'S OFFICE. THIS DRAWING IS TO BE READ & UNDERSTOOD IN CONJUNCTION WITH THE STRUCTURAL, MECHANICAL, ELECTRICAL & / OR ANY OTHER CONSULTANT'S DOCUMENTATION AS MAY BE APPLICABLE TO THE PROJECT PRIOR TO THE START OF ANY WORKS AND FOR ITS DURATION.


PROJECT:
**25 Yabunaru Street
Austral**
Lot 527 in DP1310900 at 25
Yabunaru Street Austral NSW 2179

DRAWING TITLE:
SECTIONS

NORTH:

LOT NO:	DATE:	SCALE:	DRAWING No:	REV:
527	8-09-2026	1 : 100	CC.10	6
DRAWN BY:	CHECKED BY:			ISSUED BY:
AS	RH			
DRAFTED BY:	CLIENT NAME:			
SL	Gokul Prasad Prasai & Sunita Karki Prasai			

CC ISSUE

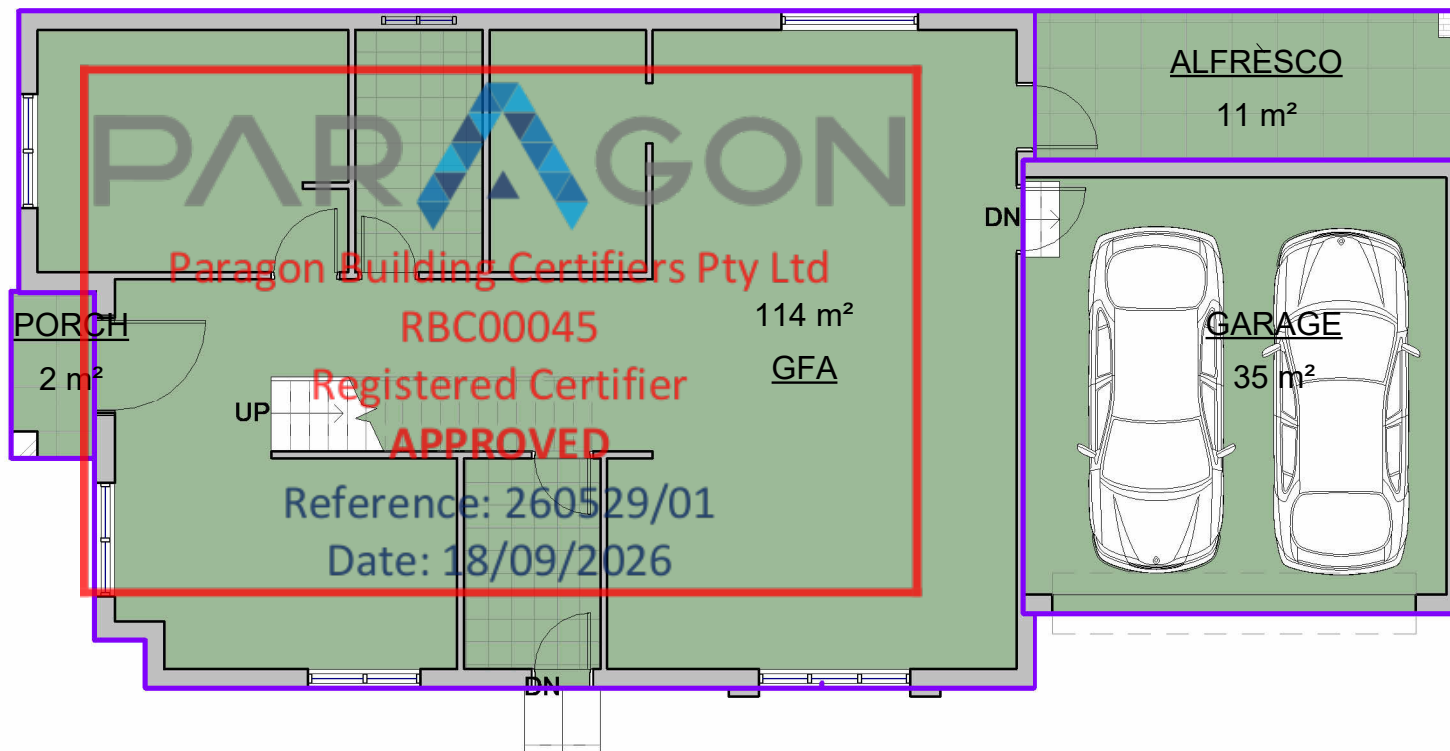

1 Ground Floor
1 : 100

FLOOR PLAN(GROSS)	
Name	Area

Ground Floor

GFA	114 m²
PORCH	2 m²
ALFRESCO	11 m²
GARAGE	35 m²


Ground Floor: 4 162 m²

First Floor

FFA	96 m²
BALCONY	7 m²
VOID	14 m²

First Floor: 3 117 m²

Grand total: 7 280 m²

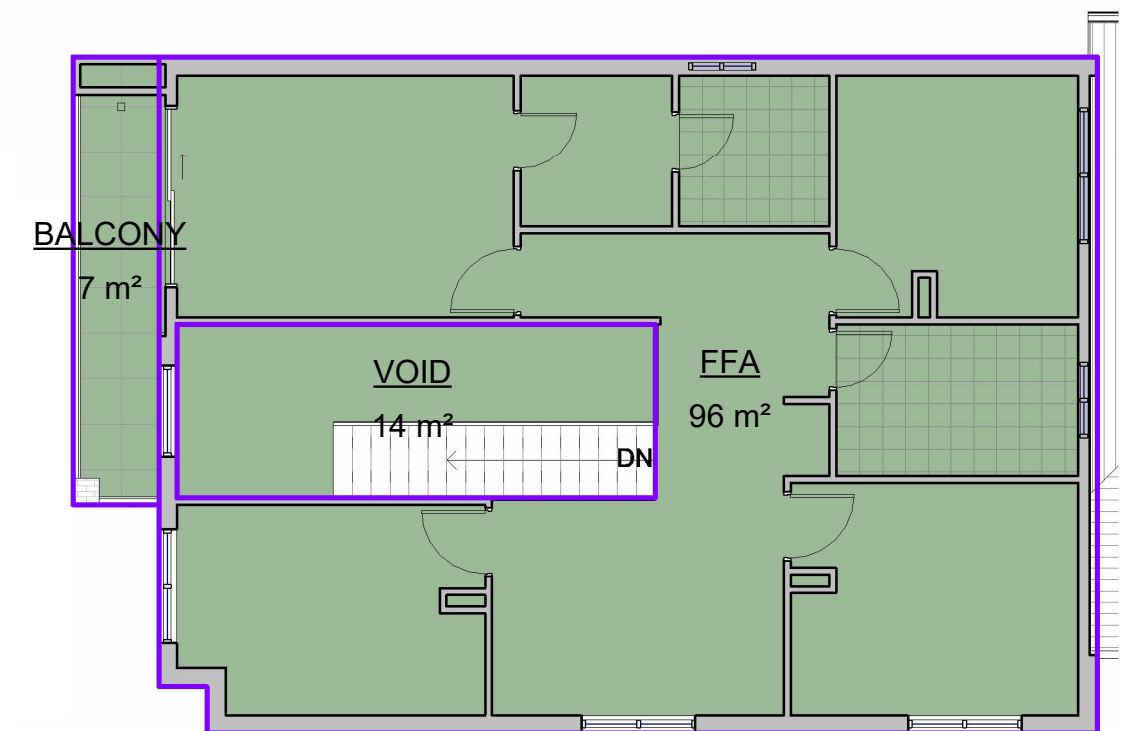

2 First Floor
1 : 100


REV	DATE	DESCRIPTION	BY
6	7-09-2026	CC-ISSUE	
5	26-08-2026	DA - Additional Information	
4	6-08-2026	DA ISSUE	
3	29-04-2026	Brick finish to wall and foam render finish to parapet and cladding wall - Ek	
1	02-04-2026	Bank Set	



 THIS DRAWING IS THE EXCLUSIVE PROPERTY OF THE DEVELOPER & THE REPRODUCTION OF ANY PART WITHOUT THE PRIOR WRITTEN CONSENT OF THE DEVELOPER IS A VIOLATION OF APPLICABLE LAWS. IN NO EVENT SHALL THE DEVELOPER BE HELD LIABLE FOR SPECIAL COLLATERAL, INCIDENTAL OR CONSEQUENTIAL LIABILITY IN CONNECTION WITH THE USE OF THIS DIGITAL DATA ONCE RELEASED FROM THE DEVELOPER'S OFFICE. THIS DRAWING IS TO BE READ & UNDERSTOOD IN CONJUNCTION WITH THE STRUCTURAL, MECHANICAL, ELECTRICAL & / OR ANY OTHER CONSULTANT'S DOCUMENTATION AS MAY BE APPLICABLE TO THE PROJECT PRIOR TO THE START OF ANY WORKS AND FOR ITS DURATION.

PROJECT:
25 Yabunaru Street
Austral
 Lot 527 in DP1310900 at 25
 Yabunaru Street Austral NSW 2179

DRAWING TITLE:
GROSS AREA PLAN

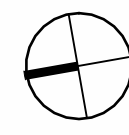
NORTH:


LOT NO:
527
 DRAWN BY:
AS
 DRAFTED BY:
SL

DATE:
8-09-2026
 CHECKED BY:
RH
 CLIENT NAME:
Gokul Prasad Prasai & Sunita Karki Prasai

SCALE:
1 : 100

CC ISSUE
 DRAWING No: **CC.11**
 REV: **6**
 ISSUED BY:

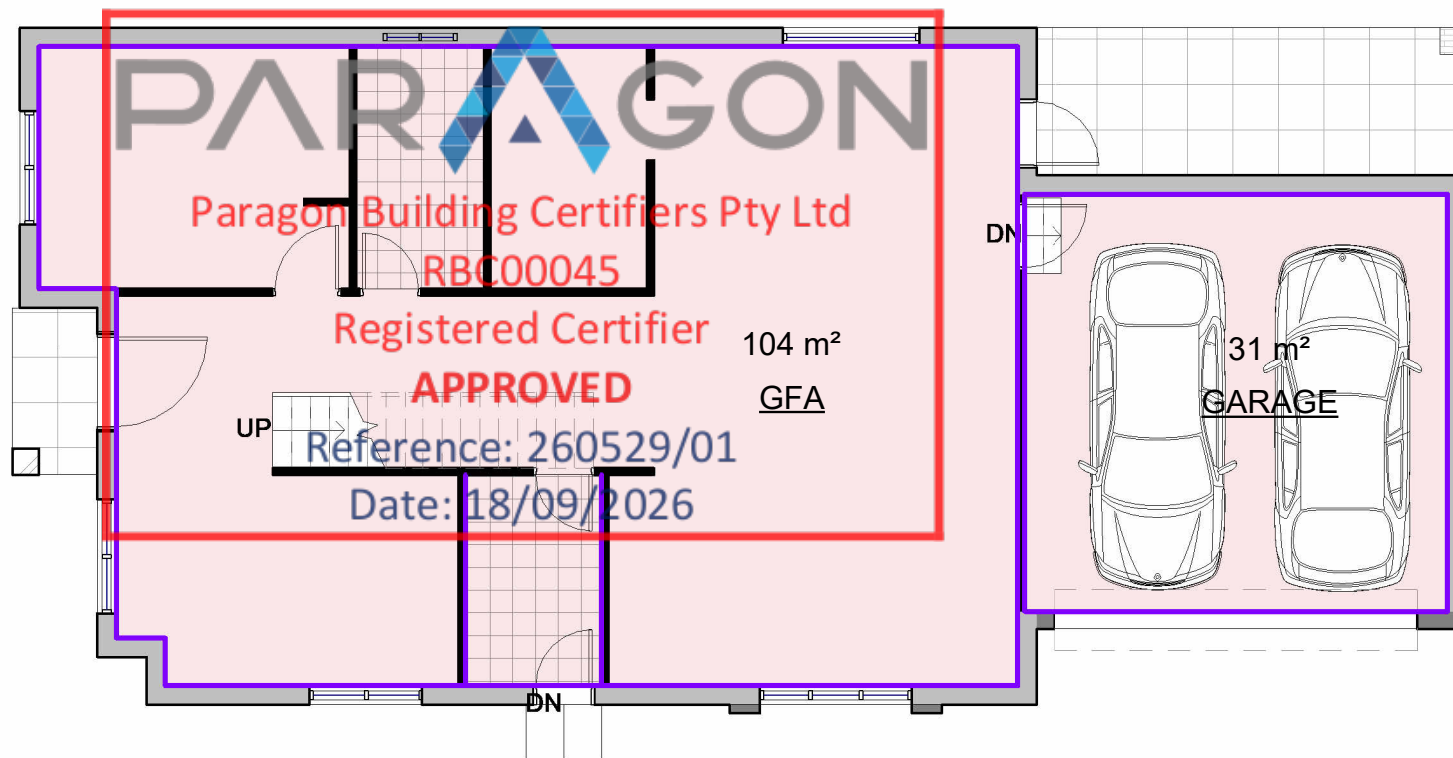

Area Schedule (Rentable)	
Name	Area

Ground Floor

GFA	104 m ²
GARAGE	31 m ²

Ground Floor: 2 134 m²

First Floor

FFA	86 m ²
STAIRCASE/VOID	14 m ²


First Floor: 2 100 m²

Grand total: 4 235 m²

1

Ground Floor

1 : 100

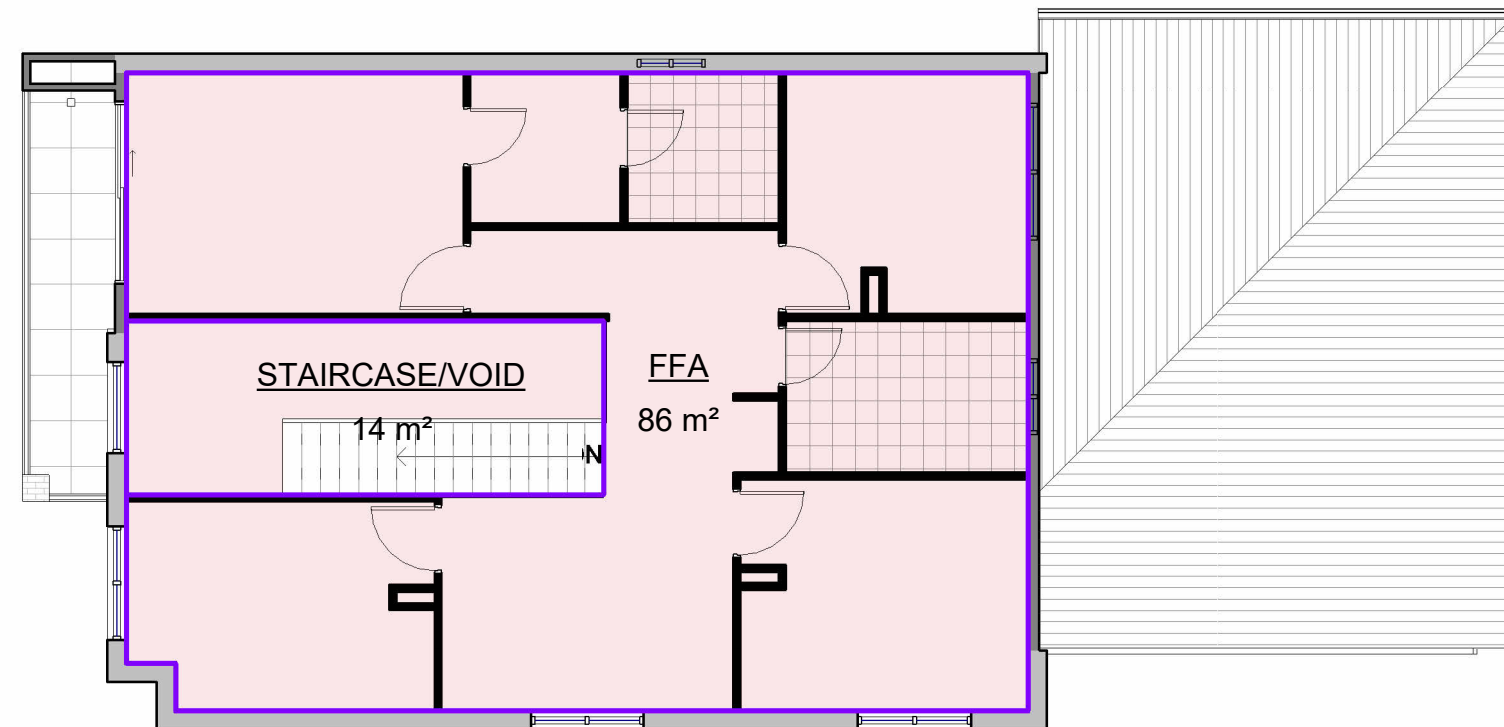

2

First Floor

1 : 100


REV	DATE	DESCRIPTION	BY
6	7-09-2026	CC-ISSUE	
5	26-08-2026	DA - Additional Information	
4	6-08-2026	DA ISSUE	
3	29-04-2026	Brick finish to wall and foam render finish to parapet and cladding wall - Ek	




THIS DRAWING IS THE EXCLUSIVE PROPERTY OF THE DEVELOPER & THE REPRODUCTION OF ANY PART WITHOUT THE PRIOR WRITTEN CONSENT OF THE DEVELOPER IS A VIOLATION OF APPLICABLE LAWS. IN NO EVENT SHALL THE DEVELOPER BE HELD LIABLE FOR SPECIAL COLLATERAL, INCIDENTAL OR CONSEQUENTIAL LIABILITY IN CONNECTION WITH THE USE OF THIS DIGITAL DATA ONCE RELEASED FROM THE DEVELOPER'S OFFICE. THIS DRAWING IS TO BE READ & UNDERSTOOD IN CONJUNCTION WITH THE STRUCTURAL, MECHANICAL, ELECTRICAL & / OR ANY OTHER CONSULTANT'S DOCUMENTATION AS MAY BE APPLICABLE TO THE PROJECT PRIOR TO THE START OF ANY WORKS AND FOR ITS DURATION.

PROJECT:
25 Yabunaru Street
Austral
 Lot 527 in DP1310900 at 25 Yabunaru Street Austral NSW 2179

DRAWING TITLE:
RENTABLE AREA
PLAN

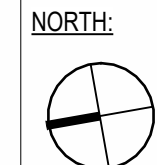

LOT NO: 527	DATE: 8-09-2026	SCALE: 1 : 100	DRAWING No: CC.12	REV: 6
DRAWN BY: AS	CHECKED BY: RH			ISSUED BY:
DRAFTED BY: SL	CLIENT NAME: Gokul Prasad Prasai & Sunita Karki Prasai			

CC ISSUE



Paragon Building Certifiers Pty Ltd


RBC00045

Registered Certifier

APPROVED


Reference: 260529/01

Date: 18/09/2026

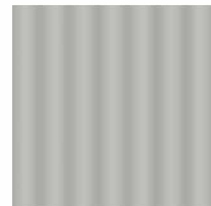

1.RF

Manufacturer: Colorbond®
Range:Mini ORB
Finish : Shale Grey
or Similar

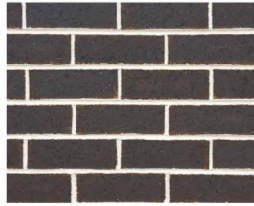

2. BR1

Manufacturer:Austral Bricks
Range:Wilderness Design
Colour Details:Blackbutt
Code:SKU 410750021420000328100
or Similar



3. CR1

Manufacturer:Austral Bricks
Range:Everyday Life Engage
Colour Details:Engage
Code:SKU 210250011130000301100
or Similar



4. CD1

Manufacturer: JamesHardie
Range:Weatherboard
Product Details:Hardie Plank
Smooth Finish
Finish : Paint Finish (Taubmans -
Opulent White or Similar white and
Neutral colour)




5. AL

Windows and Sliding Door
Manufacturer: ABM Door & Window
Finish : Monument



6. GD

Manufacturer: Door Works
Range:Flat Panel
Product Details:Colorbond® is
a high-quality, pre-painted
steel product
Finish : Woodgrain Colorbond-
Dover White

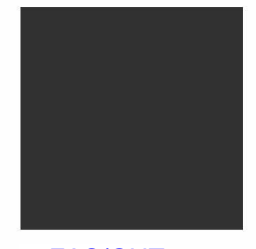

7. FAS/GUT

Gutter fascia,gutter
Manufacturer: Colorbond®
Finish : Monument

NOTE : ALL COLOURS SPECIFIED ARE INDICATIVE ONLY AND ARE SUBJECT TO VARIATION AND TO AVAILABILITY
ANY DISCREPANCY PLEASE FOLLOW AS PER RENDERED IMAGE

REV	DATE	DESCRIPTION	BY
6	7-09-2026	CC-ISSUE	
5	26-08-2026	DA - Additional Information	
4	6-08-2026	DA ISSUE	
3	29-04-2026	Brick finish to wall and foam render finish to parapet and cladding wall - Ek	



THIS DRAWING IS THE EXCLUSIVE PROPERTY OF THE DEVELOPER & THE REPRODUCTION OF ANY PART WITHOUT THE PRIOR WRITTEN CONSENT OF THE DEVELOPER IS A VIOLATION OF APPLICABLE LAWS. IN NO EVENT SHALL THE DEVELOPER BE HELD LIABLE FOR SPECIAL COLLATERAL, INCIDENTAL OR CONSEQUENTIAL LIABILITY IN CONNECTION WITH THE USE OF THIS DIGITAL DATA ONCE RELEASED FROM THE DEVELOPER'S OFFICE. THIS DRAWING IS TO BE READ & UNDERSTOOD IN CONJUNCTION WITH THE STRUCTURAL, MECHANICAL, ELECTRICAL & / OR ANY OTHER CONSULTANT'S DOCUMENTATION AS MAY BE APPLICABLE TO THE PROJECT PRIOR TO THE START OF ANY WORKS AND FOR ITS DURATION.


PROJECT:
25 Yabunaru Street
Austral
Lot 527 in DP1310900 at 25
Yabunaru Street Austral NSW 2179

DRAWING TITLE:
COLOR SCHEDULE

NORTH:

LOT NO:	527	DATE:	8-09-2026	SCALE:		DRAWING No:	CC.13	REV:	6
DRAWN BY:	AS	CHECKED BY:	RH					ISSUED BY:	
DRAFTED BY:	SL	CLIENT NAME:	Gokul Prasad Prasai & Sunita Karki Prasai						

CC ISSUE

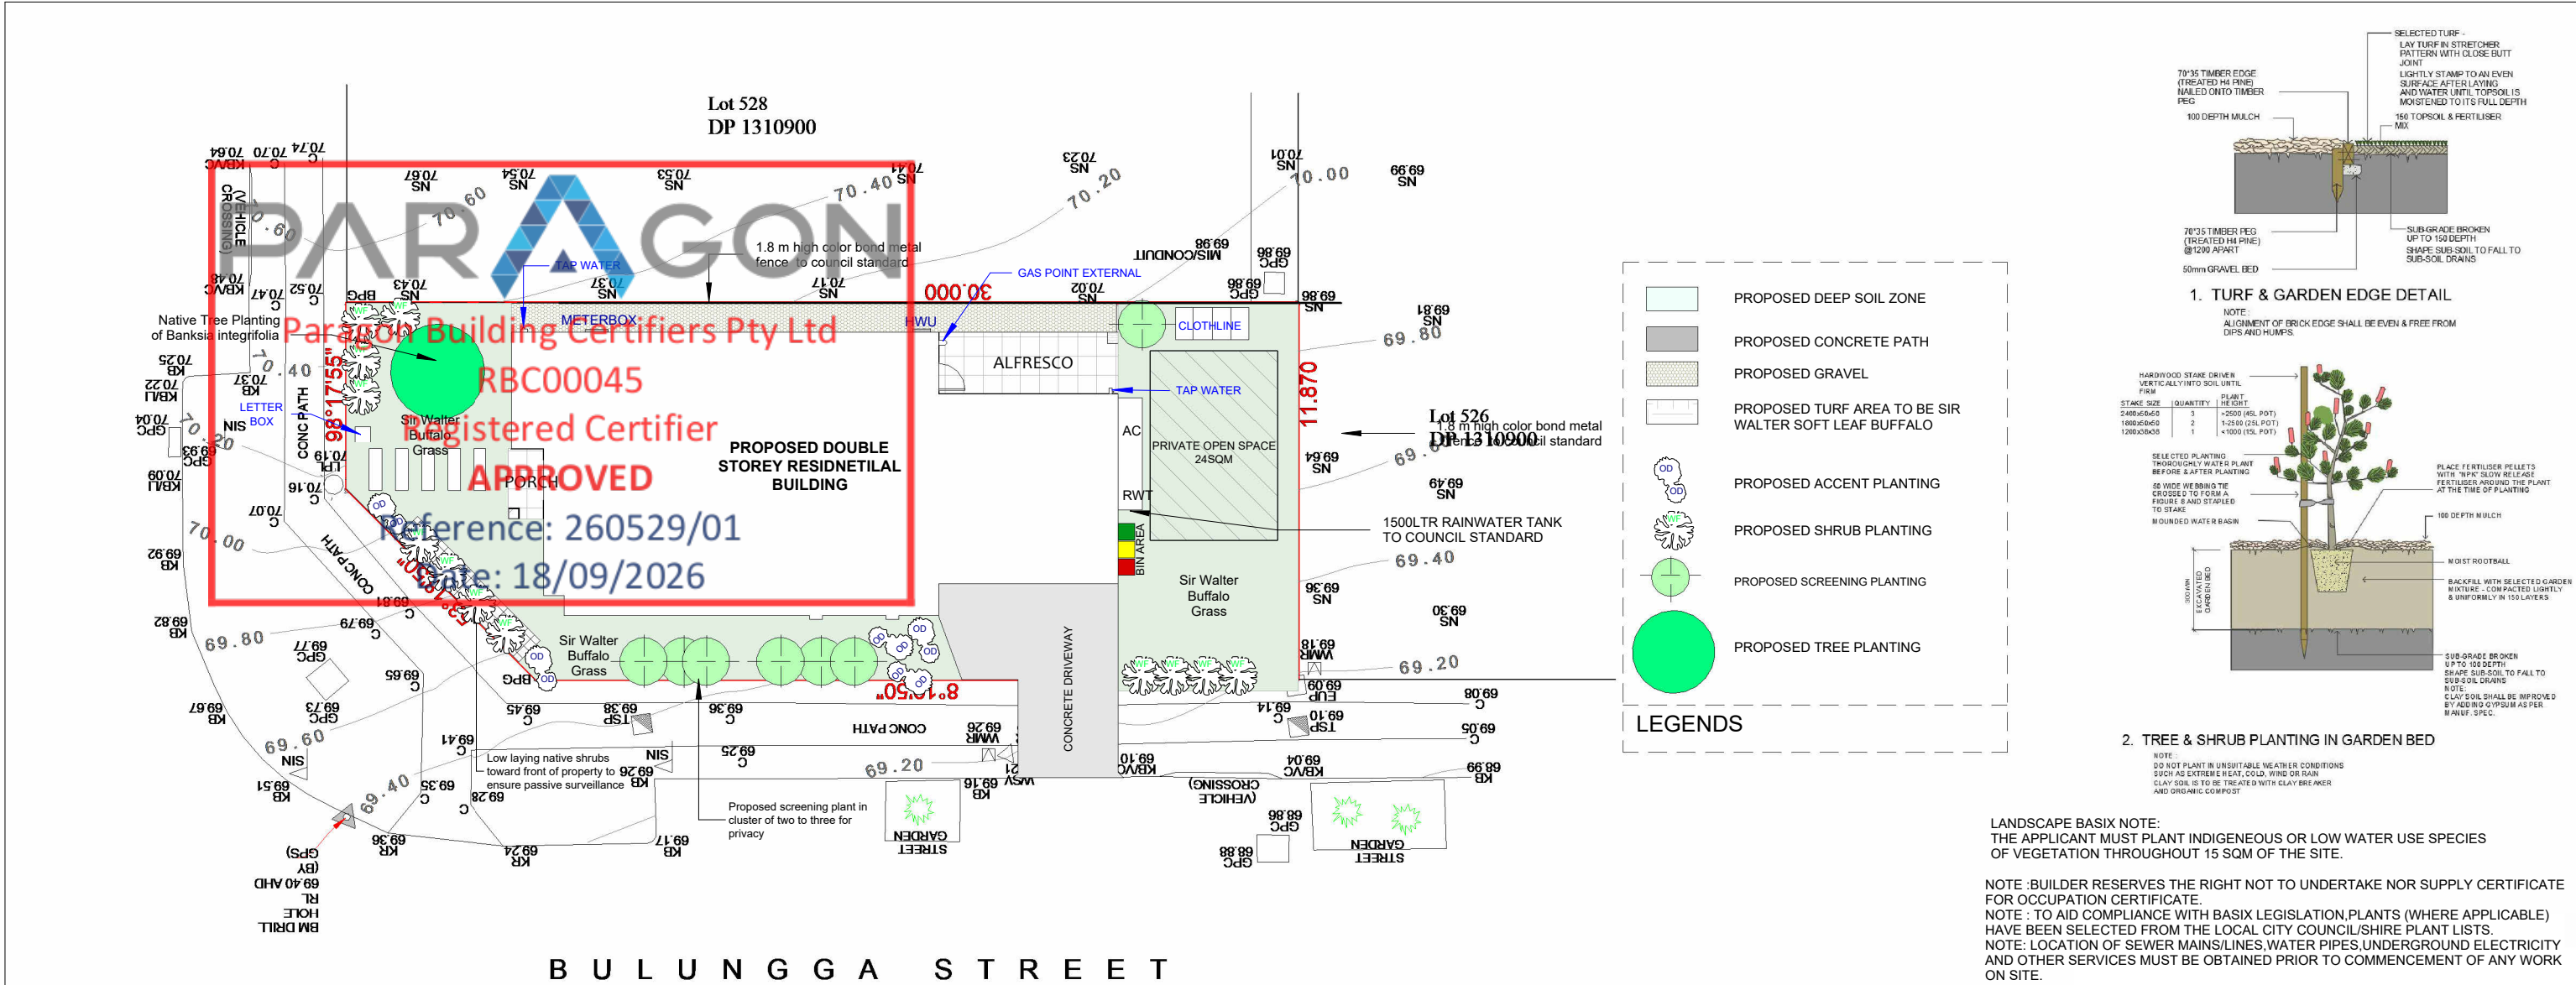

LANDSCAPE PLAN
1 : 200

PLANT SCHEDULE

Genus	Common Name	Qty	Pot size	Height	width
Trees					
Banksia integrifolia	coast banksia	1	45L	7	4
Cupaniopsis anacardioides	Tuckeroo	1	45L	8	4
Shrubs					
Grevillea 'moonlight'	Grevillea Moonlight	-	140mm	3	1.5
Leptospermum 'Cardwell'	Tea Tree	-	140mm	1.5	1
Leucophyta Brownii	Cushion Bush	-	140mm	1.5	1
Westringia Fruticosa	Coastal Rosemary	-	140mm	1.5	2
Accents					
Agave Americana	American Aloe	-	200mm	1.5	1.5

LANDSCAPE AREA

FRONT AREA	73.9 m ²
REAR AREA	69.6 m ²

REV	DATE	DESCRIPTION	BY
6	7-09-2026	CC-ISSUE	
5	26-08-2026	DA - Additional Information	
4	6-08-2026	DA ISSUE	
3	29-04-2026	Brick finish to wall and foam render finish to parapet and cladding wall - Ek	

RUBY HOMES

THIS DRAWING IS THE EXCLUSIVE PROPERTY OF THE DEVELOPER & THE REPRODUCTION OF ANY PART WITHOUT THE PRIOR WRITTEN CONSENT OF THE DEVELOPER IS A VIOLATION OF APPLICABLE LAWS. IN NO EVENT SHALL THE DEVELOPER BE HELD LIABLE FOR SPECIAL COLLATERAL, INCIDENTAL OR CONSEQUENTIAL LIABILITY IN CONNECTION WITH THE USE OF THIS DIGITAL DATA ONCE RELEASED FROM THE DEVELOPER'S OFFICE. THIS DRAWING IS TO BE READ & UNDERSTOOD IN CONJUNCTION WITH THE STRUCTURAL, MECHANICAL, ELECTRICAL & / OR ANY OTHER CONSULTANT'S DOCUMENTATION AS MAY BE APPLICABLE TO THE PROJECT PRIOR TO THE START OF ANY WORKS AND FOR ITS DURATION.

PROJECT:
25 Yabunaru Street
Austral
Lot 527 in DP1310900 at 25 Yabunaru Street Austral NSW 2179

DRAWING TITLE:
LANDSCAPE PLAN



CC ISSUE					
LOT NO:	527	DATE:	8-09-2026	SCALE:	1 : 200
DRAWN BY:	AS	CHECKED BY:	RH	DRAWING No:	CC.14
DRAFTED BY:	SL	CLIENT NAME:	Gokul Prasad Prasai & Sunita Karki Prasai		
				REV:	6
				ISSUED BY:	

ABCB HOUSING PROVISIONS : PART 10.2 WET AREA WATERPROOFING

10.2.1 Wet Areas

- 1. Building elements in wet areas within a building must be protected with a waterproofing system.
- 2. The waterproofing system in (1) must be either waterproof or water resistant in accordance with 10.2.2 to 10.2.6.

10.2.2 Shower Area (enclosed and unenclosed)

- 1. For a shower area with a hob, step-down or level threshold, the following applies:
 - a. The floor of the shower area must be waterproof, including any hob or step-down (see Figure 10.2.2); and
 - b. The walls of the shower area must be waterproof not less than 1800 mm above the floor substrate (see Figure 10.2.2).
 - c. Wall junctions and joints within the shower area must be waterproof not less than 40 mm either side of the junction (see Figure 10.2.2).
 - d. Wall/floor junctions within the shower area must be waterproof (see Figure 10.2.2).
 - e. Penetrations within the shower area must be waterproof.
- 2. A shower with a preformed shower base must also comply with the requirements of (1), except for (a) which is not applicable.

Figure 10.2.2: Extent of treatment for shower areas - concrete compressed fibre-cement and fibre-cement sheet floors.

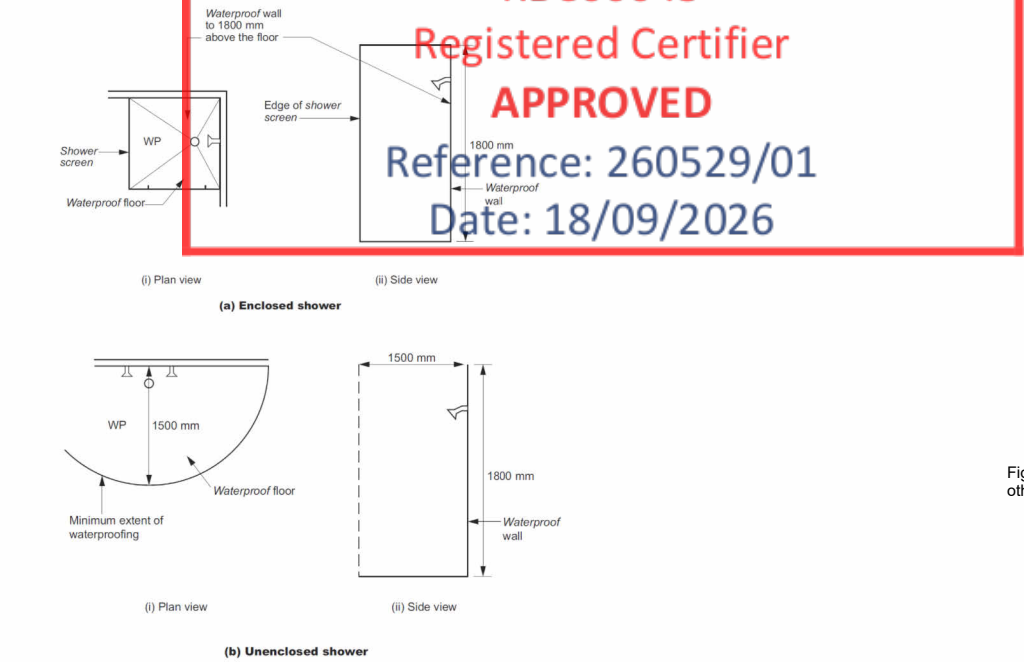


Figure Notes
Wall/floor junction heights are to be as per 10.2.2 to 10.2.6 (as applicable).

Notes
Where a shower is above a bath or spa, use requirements for shower.

10.2.3 Area outside shower area

- 1. For concrete, compressed fibre-cement and fibre-cement sheet flooring, the floor of the room must be water resistant.
- 2. For timber floors including particleboard, plywood and other timber based flooring materials, the floor of the room must be waterproof.
- 3. Wall/floor junctions must be -
 - a. waterproof, and
 - b. where a flashing is used, the horizontal leg must be not less than 40 mm.

10.2.4 Areas adjacent to baths and spas without showers

- 1. For areas adjacent to all baths and spas, the following applies:
 - a. For concrete, compressed fibre-cement and fibre-cement sheet flooring, the floor of the room must be water resistant.
 - b. For timber floors including particleboard, plywood and other timber based flooring materials, the floor of the room must be waterproof.
 - c. Tap and spout penetrations must be waterproof where they occur in horizontal surfaces.
- 2. For areas adjacent to non-freestanding baths and spas, the following applies:
 - a. Walls must be water resistant (see Figure 10.2.4a and Figure 10.2.4b)-
 - to a height of not less than 150mm above the vessel, for the extent of the vessel, where the vessel is within 75mm of a wall; and
 - for all exposed surfaces below vessel lip.
 - b. Wall junctions and joints must be water resistant within 150mm above a vessel for the extent of the vessel.
 - c. Wall/floor junctions must be waterproof for the extent of the vessel (see Figure 10.2.4a and Figure 10.2.4b).
- 3. For inserted baths and spas, the following applies:
 - a. For floors and horizontal surfaces:
 - Any shelf area adjoining the bath or spa must be waterproof and include a waterstop under the vessel lip.
 - There are no requirements for the floor under a bath or spa.
 - b. For walls:
 - Waterproof to not less than 150mm above the lip of a bath or spa.
 - There are no requirements for the floor under a bath or spa.
 - c. For wall junctions and joints, the following applies:
 - Waterproof junctions within 150mm of a bath or spa.
 - There are no requirements for junctions and joints in walls beneath the lip of a bath or spa.
 - d. Tap and spout penetrations must be waterproof where they occur in horizontal surfaces.

Figure 10.2.4a: Areas adjacent to baths and spas without showers for concrete, compressed fibre-cement and fibre-cement sheet flooring


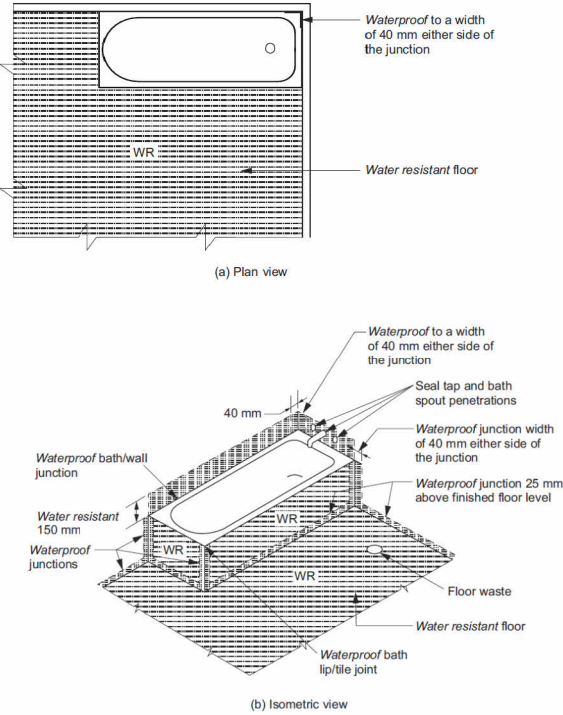



Figure 10.2.4b: Areas adjacent to baths and spas without showers for timber floors including particle-board, plywood and other floor materials

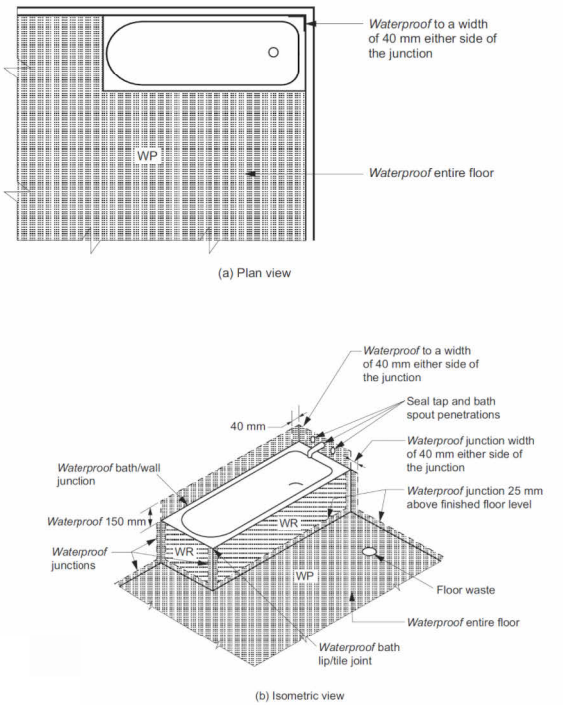

10.2.5 Other areas

- 1. For walls adjoining other types of vessels (e.g. sink, basin or laundry tub), the following applies:
 - a. Walls must be water resistant to a height of not less than 150mm above the vessel, for the extent of the vessel, where the vessel is within 75 mm of a wall (see Figure 10.2.5.)
 - b. Waterproof wall junctions where a vessel is fixed to a wall.
 - c. Waterproof tap and spout penetrations where they occur in surfaces required to be waterproof or water resistant.
- 2. For laundries and WCs, the following applies:
 - a. The floor of the room must be water resistant.
 - b. Wall/floor junctions must be water resistant, and where a flashing is used, the horizontal leg must not be less than 40 mm.
- 3. For WCs with handheld bidet spray installations, the following applies:
 - a. The floor of the room must be waterproof.
 - b. Walls must be -
 - waterproof in WC area within a 900 mm radius from the wall connection of the handheld bidet spray device to a height of not less than 150mm above the floor substrate; and
 - water resistant in WC area within a 900 mm radius from the wall connection of the handheld bidet device to not less than 1200 mm above the finished floor level of the WC.
 - c. Wall junctions within the WC area within 900 mm radius from the wall connection of the handheld bidet spray device must be waterproof.
 - d. Wall/floor junctions within the WC area within 1000 mm radius from the wall connection of the handheld bidet spray device must be waterproof.
 - e. Penetrations in the WC area must be waterproof.

Figure 10.2.5: Bath and vessel abutting wall - areas to be protected

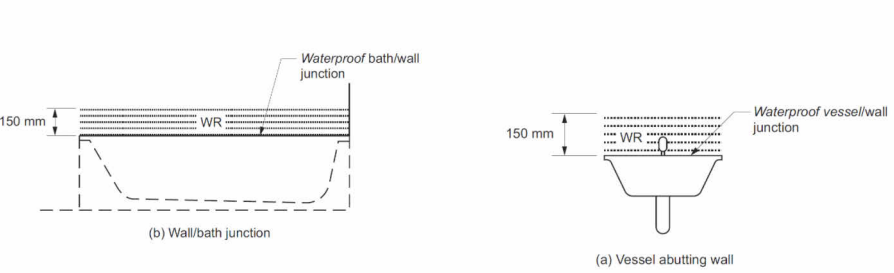

10.2.6 Waterproofing systems

- 1. For the purposes of this Part, a waterproofing system is deemed -
 - a. waterproof, if it complies with (2); or
 - b. water resistant, if it complies with (3).
- 2. For a waterproofing system required to be waterproof in accordance with 10.2.2 to 10.2.5, the materials nominated in 10.2.8 must be used.
- 3. For a waterproofing system required to be water resistant in accordance with 10.2.2 to 10.2.5, the materials nominated in 10.2.9 must be used in conjunction with the materials in 10.2.10.

10.2.12 Construction of wet area floors - falls

Where a floor waste is installed -

- a. the minimum continuous fall of a floor plane to the waste must be 1:80; and
- b. the maximum continuous fall of a floor plane to the waste must be 1:50.

				CC ISSUE			
				LOT NO:	DATE:	SCALE:	DRAWING No: REV:
6	7-09-2026	CC-ISSUE		527	8-09-2026	1 : 50	CC.15 6
5	26-08-2026	DA - Additional Information		DRAWN BY:	CHECKED BY:		
4	6-08-2026	DA ISSUE		AS	RH		
3	29-04-2026	Brick finish to wall and foam render finish to parapet and cladding wall - Ek		DRAFTED BY:	CLIENT NAME:		
REV	DATE	DESCRIPTION	BY	SL	Gokul Prasad Prasai & Sunita Karki Prasai		



THIS DRAWING IS THE EXCLUSIVE PROPERTY OF THE DEVELOPER & THE REPRODUCTION OF ANY PART WITHOUT THE PRIOR WRITTEN CONSENT OF THE DEVELOPER IS A VIOLATION OF APPLICABLE LAWS. IN NO EVENT SHALL THE DEVELOPER BE HELD LIABLE FOR SPECIAL COLLATERAL, INCIDENTAL OR CONSEQUENTIAL LIABILITY IN CONNECTION WITH THE USE OF THIS DIGITAL DATA ONCE RELEASED FROM THE DEVELOPER'S OFFICE. THIS DRAWING IS TO BE READ & UNDERSTOOD IN CONJUNCTION WITH THE STRUCTURAL, MECHANICAL, ELECTRICAL & / OR ANY OTHER CONSULTANT'S DOCUMENTATION AS MAY BE APPLICABLE TO THE PROJECT PRIOR TO THE START OF ANY WORKS AND FOR ITS DURATION.

PROJECT:
25 Yabunaru Street
Austral
Lot 527 in DP1310900 at 25 Yabunaru Street Austral NSW 2179

DRAWING TITLE:
WATERPROOFING DETAILS

NORTH:

