

FOR CONSTRUCTION

LOT 10 IN DP 263073

LOCATED AT No.17 ADAM PLACE MACQUARIE FIELDS NSW 2564

Demolition of Existing Dwelling and Construction of a Two-Storey Residential Dwelling with Attached Double Garage and Attached Secondary Dwelling, Including Associated Site Works

Paragon Building Certifiers Pty Ltd


RBC00045

Registered Certifier

APPROVED

Reference: 260403/01

Date: 03/08/2026

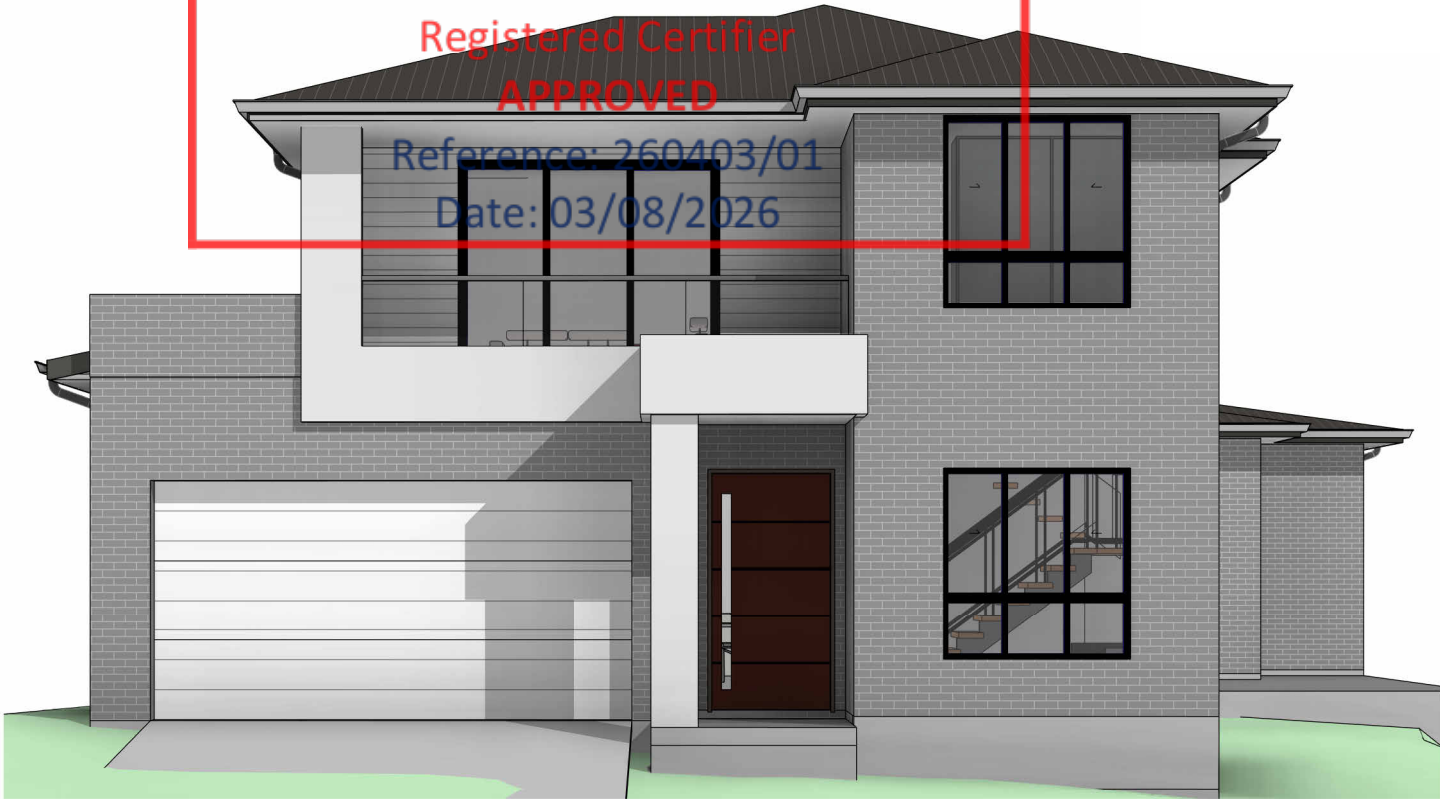

GENERAL LEGEND

AC	AIR CONDITIONING UNIT
AL	POWDERCOATED ALUMINIUM DOOR/ WINDOW
BAL	BALUSTRADE TYPE
BG	BOX GUTTER
BR1, BR2, etc.	BRICK FACE TYPE
CAP	METAL CAPPING
CD1, CD2, etc.	WALL CLADDING
CONC.	CONCRETE FLOOR
CPT	CARPET
CRT	CONCRETE ROOF TILES
CR1, CR2, etc.	CEMENT RENDER TYPE/ COLOUR
DP/S	DOWN PIPE
DW	DISH WASHER
ED	ENTRY DOOR
F	FRIDGE
FAS	FASCIA
FET	FEATURE TILE
FT, FT1, FT2, etc.	FLOOR TILES
FW	FLOOR WASTE
GD	GARAGE DOOR
GUT	GUTTER
HWU	HOT WATER UNIT
HYB	HYBRID FLOOR
L	LINEN
MR	METAL ROOF
MW	MICROWAVE OVEN
NGL	NATURAL GROUND LEVEL
OBS	OBSCURED GLASS
P	PANTRY
R	ROBE
RL	REDUCED LEVEL
RWH	RAIN WATER HEAD
RWT	RAIN WATER TANK
S	STORAGE
TOW	TOP OF WALL
TL	TIMBER LAMINATE
WC	WATER CLOSET
WM	WASHING MACHINE
SD	SMOKE DETECTOR

Sheet List			
Sheet No.	Sheet Name	Drawn By	Checked By
CC.01	COVER SHEET	ROHIT	RH
CC.02A	GENERAL NOTES	ROHIT	RH
CC.02B	GENERAL NOTES B	ROHIT	RH
CC.03A	LOCATION PLAN AND SITE PLAN	ROHIT	RH
CC.03B	SITE CUT/FILL PLAN	ROHIT	RH
CC.04	SITE ANALYSIS AND SEDIMENT CONTROL	ROHIT	RH
CC.05	GROUND FLOOR PLAN	AS	RH
CC.06	FIRST FLOOR LEVEL	AS	RH
CC.07	ROOF PLAN	AS	RH
CC.08	ELEVATION 01	ROHIT	RH

Sheet List			
Sheet No.	Sheet Name	Drawn By	Checked By
CC.09	ELEVATION 02	ROHIT	RH
CC.10	SECTIONS	ROHIT	RH
CC.11	AREA CALCULATION PLAN	ROHIT	RH
CC.12	ROOM AREA PLAN	ROHIT	RH
CC.13	COLOR SCHEDULE	ROHIT	RH
CC.14	LANDSCAPE PLAN	ROHIT	RH
CC.15	BASIX COMMITMENTS	RUBY	RH
CC.15B	BASIX CERTIFICATES	RUBY	RH
CC.16	DOOR WINDOW SCHEDULE	AS	RH
CC.17	WATERPROOFING NOTES	AS	RH
CC.19	DEMOLITION PLAN	ROHIT	RH
CC.20	SEPARATING WALL DETAILS	AS	RH

BASIX™Certificate

Building Sustainability Index
www.planningportal.nsw.gov.au/development-and-assessment/basix

Multi Dwelling

Certificate number: 15637958

This certificate confirms that the proposed development will meet the NSW government's requirements for sustainability, if it is built in accordance with the commitments set out below. Terms used in this certificate, or in the commitments, have the meaning given by the document entitled "BASIX Definitions" dated 10/09/2020 published by the Department. This document is available at www.planningportal.nsw.gov.au/development-and-assessment/basix

Secretary
Date of issue: Monday, 27 April 2026
To be valid, this certificate must be submitted with a development application or lodged with a complying development certificate application, it must be accompanied by NatHERS certificate 0012947660

NSW

When submitting this BASIX certificate with a development application or complying development certificate application, it must be accompanied by NatHERS certificate 0012947660

Project summary

Project name	Basix 17 Adam Place Macquarie Fields 2564
Owner address	17 ADAM PLACE MACQUARIE FIELDS 2564
Local Government area	CAMPBELLTOWN
Plan type and plan number	Deposited Plan: 263073
Lot No.	10
Section no.	1
No. of residential lot buildings	0
Residential lot buildings no. of dwellings	0
Multi-lotting housing no. of dwellings	2
No. of single dwelling houses	0

Project score

Water	40	Target 40
Thermal Performance	Pass	Target Pass
Energy	74	Target 70
Materials	43	Target n/a

Certificate Prepared by

Name: Zoran Cvetkovski	SUSTAINABILITY-2 PTY LIMITED
ABN 61 5962311955	

Certificate No. 0012947660

Scan QR code or follow website link for rating details.

Assessor name Zoran Cvetkovski

Accreditation No. DMN/13/1641

Property Address 17 Adam Place, Macquarie Fields NSW, 2564

hstar.com.au/QR/Generate?p=ELTMXGeDB

Version 2025.0

NOTE.: ALL IMAGES ARE FOR ILLUSTRATION ONLY AND ARE SUBJECT TO VARIATION AND TO AVAILABILITY OF MATERIALS.

11				CC ISSUE			
REV	DATE	DESCRIPTION	BY	LOT NO:	DATE:	SCALE:	DRAWING No:
				10	21-07-2026	1 : 100	CC.01
				DRAWN BY: ROHIT	CHECKED BY: RH		
				DRAFTED BY: ROHIT	CLIENT NAME: Anila Gurung & Amodh Gurung		

PROJECT:

Residential Building

LOT 10 IN DP 263073

No.17 ADAM PLACE MACQUARIE FIELDS NSW 2564

DRAWING TITLE:

COVER SHEET

NORTH:

LOT NO:

10

DATE:

21-07-2026

SCALE:

1 : 100

DRAWING No:

CC.01

REV:

11

ISSUED BY:

BUILDING SPECIFICATIONS

National Construction Code – Volume 2,
Amendment 1 – Building Code of Australia 2022
& Housing Provisions Standard 2022

SITE PREPARATION

- PART 3.1 OF THE NCC VOLUME 2, AMENDMENT 1 - BUILDING CODE OF AUSTRALIA 2022 & HOUSING PROVISIONS STANDARD 2022.

EARTHWORKS

- TO BE CARRIED OUT IN ACCORDANCE WITH THE REQUIREMENTS OF THE ENVIRONMENTAL PLANNING & ASSESSMENT ACT 1979 AND DEVELOPMENT CONSENT CONDITIONS
- PART 3.2 OF THE NCC VOLUME 2, AMENDMENT 1 - BUILDING CODE OF AUSTRALIA 2022 & HOUSING PROVISIONS STANDARD 2022
- AS 4678:2002 - EARTH-RETAINING STRUCTURES

DRAINAGE

- PART 3.3 OF THE NCC VOLUME 2, AMENDMENT 1 - BUILDING CODE OF AUSTRALIA 2022 & HOUSING PROVISIONS STANDARD 2022.
- AS/NZS 3500.1:2021 - PLUMBING & DRAINAGE - WATER SERVICES
- AS/NZS 3500.2:2021 - PLUMBING & DRAINAGE - SANITARY PLUMBING & DRAINAGE
- AS/NZS 3500.3:2021 - PLUMBING & DRAINAGE STORMWATER DRAINAGE
- AS/NZS 3500.4:2021 - PLUMBING & DRAINAGE - HEATED WATER SERVICES

STRUCTURAL WORK

- Part 2.2 OF THE NCC VOLUME 2, AMENDMENT 1 - BUILDING CODE OF AUSTRALIA 2022 & HOUSING PROVISIONS STANDARD 2022.
- AS 4100-2020- STEEL STRUCTURES CODES
- AS/NZS 1170.0-2002 – GENERAL PRINCIPLES
- ASNZS 1170.1-2002 – PARTS 1 PERMANENT, IMPOSED AND OTHER ACTIONS
- AS/NZS 1170.2-2021 – PART 2 WIND ACTIONS
- AS 3700-2018- SAA MASONRY CODE
- AS 1684.3-2021- RESIDENTIAL TIMBER FRAMED CONSTRUCTION

FOOTINGS & SLABS

- PART 4 OF THE NCC VOLUME 2, AMENDMENT 1 - BUILDING CODE OF AUSTRALIA 2022 & HOUSING PROVISIONS STANDARD 2022.
- AS 2159:2009 - PILING - DESIGN & INSTALLATION
- AS 2870:2011 - RESIDENTIAL SLABS & FOOTINGS
- AS 3600:2018 - CONCRETE STRUCTURES

MASONRY

- PART 5 OF THE NCC VOLUME 2, AMENDMENT 1 - BUILDING CODE OF AUSTRALIA 2022 & HOUSING PROVISIONS STANDARD 2022.
- AS 3700:2018 - MASONRY STRUCTURES
- PART 6 OF THE NCC VOLUME 2, AMENDMENT 1 - BUILDING CODE OF AUSTRALIA 2022 & HOUSING PROVISIONS STANDARD 2022.
- AS 1684.2:2021 - RESIDENTIAL TIMBER-FRAMED CONSTRUCTION - NON- CYCLONIC AREAS
- AS 1720.1:2010 - TIMBER STRUCTURES - DESIGN METHODS
- AS 4100:2020 - STEEL STRUCTURES
- AS 3660.1-2014 – TERMITE MANAGEMENT SYSTEM

ROOF & WALL CLADDING

- PART 7 OF THE NCC VOLUME 2, AMENDMENT 1 - BUILDING CODE OF AUSTRALIA 2022 & HOUSING PROVISIONS STANDARD 2022.
- AS 1273:1991 - UNPLASTICIZED PVC (UPVC) DOWNPIPES & FITTINGS FOR RAINWATER
- AS 1562.1:2018 - DESIGN & INSTALLATION OF SHEET ROOF & WALL CLADDING - METAL
- AS/NZS 1562.3:2006 - DESIGN & INSTALLATION OF SHEET ROOF & WALL CLADDING - PLASTIC
- AS 2049:2002 - ROOF TILES
- AS 2050:2018 - INSTALLATION OF ROOF TILES
- AS 4285:2019 – ROOFLIGHTS

GLAZING

- PART 8 OF THE NCC VOLUME 2, AMENDMENT 1 - BUILDING CODE OF AUSTRALIA 2022 & HOUSING PROVISIONS STANDARD 2022.
- AS 1288:2021 - GLASS IN BUILDINGS -SELECTION & INSTALLATION
- AS 2047:2014 - WINDOWS & EXTERNAL GLAZED DOORS IN BUILDINGS
- AS/NZS 2208:1996 - SAFETY GLAZING MATERIALS IN BUILDINGS

FIRE SAFETY

- PART 9 OF THE NCC VOLUME 2, AMENDMENT 1 - BUILDING CODE OF AUSTRALIA 2022 & HOUSING PROVISIONS STANDARD 2022.
- AS 3786:2014 - SMOKE ALARMS USING SCATTERED LIGHT, TRANSMITTED LIGHT OR IONIZATION

HEALTH & AMENITY

- PART 10 OF THE NCC VOLUME 2, AMENDMENT 1 - BUILDING CODE OF AUSTRALIA 2022 & HOUSING PROVISIONS STANDARD 2022.
- AS/NZS ISO 717.1:2004 - ACOUSTICS - RATING OF SOUND INSULATION IN BUILDINGS & OF BUILDING ELEMENTS -AIRBORNE SOUND INSULATION
- AS ISO 717.2:2004 - ACOUSTICS - RATING OF SOUND INSULATION IN BUILDINGS & OF BUILDING ELEMENTS - IMPACT SOUND INSULATION
- AS 1668.2:2012 - THE USE OF VENTILATION & AIR CONDITIONING IN BUILDINGS - MECHANICAL VENTILATION IN BUILDINGS
- AS 1668.4:2012 - THE USE OF VENTILATION & AIR CONDITIONING IN BUILDINGS - NATURAL VENTILATION OF BUILDINGS
- AS/NZS 1680.0:2009 - INTERIOR LIGHTING - SAFE MOVEMENT
- AS 3740:2021 - WATERPROOFING OF DOMESTIC WET AREAS
- AS 3000-2018 – ELECTRICAL INSTALLATION
- BCA Part 10.8.1, AS4200.1 & AS4200.2 – PLIABLE BUILDING MEMBRANE INSTALLED.

WATERPROOFING

- PART 10.2 OF THE NCC VOLUME 2, AMENDMENT 1 - BUILDING CODE OF AUSTRALIA 2022 & HOUSING PROVISIONS STANDARD 2022
- AS 3740-2021- WATERPROOFING TO WET AREA
- AS 4654-2012 – EXTERNAL WET AREAS

SAFE MOVEMENT & ACCESS

- PART 11 OF THE NCC VOLUME 2, AMENDMENT 1 - BUILDING CODE OF AUSTRALIA 2022 & HOUSING PROVISIONS STANDARD 2022.
- AS 1428.1:2009 - DESIGN FOR ACCESS & MOBILITY – GENERAL REQUIREMENTS FOR ACCESS - NEW BUILDING WORK
- AS 1657:2018 - FIXED PLATFORMS, WALKWAYS, STAIRWAYS & LADDERS - DESIGN, CONSTRUCTION & INSTALLATION

HANDRAILS & BALUSTRADE

- PART 11.3.3 OF THE NCC VOLUME 2, AMENDMENT 1 - BUILDING CODE OF AUSTRALIA 2022 & HOUSING PROVISIONS STANDARD 2022.
- PART 11.3.4 OF THE NCC VOLUME 2, AMENDMENT 1 - BUILDING CODE OF AUSTRALIA 2022 & HOUSING PROVISIONS STANDARD 2022.
- PART 11.3.5 OF THE NCC VOLUME 2, AMENDMENT 1 - BUILDING CODE OF AUSTRALIA 2022 & HOUSING PROVISIONS STANDARD 2022.
- AS 1170.1-2002 – BALUSTRADE INSTALLATION

PROTECTION OF OPENABLE WINDOW

PART 11.3.7 AND 11.3.8 OF THE NCC VOLUME 2, AMENDMENT 1 - BUILDING CODE OF AUSTRALIA 2022 & HOUSING PROVISIONS STANDARD 2022.

ENERGY EFFICIENCY

- PART 13 OF THE NCC VOLUME 2, AMENDMENT 1 - BUILDING CODE OF AUSTRALIA 2022 & HOUSING PROVISIONS STANDARD 2022 & BASIX CERTIFICATE.

HEATING APPLIANCES, FIREPLACES, CHIMNEYS AND FLUES

- PART 12.4 OF THE NCC VOLUME 2, AMENDMENT 1 - BUILDING CODE OF AUSTRALIA 2022 & HOUSING PROVISIONS STANDARD 2022.

MECHANICAL VENTILATION

- EXHAUST FROM A BATHROOM, SANITARY COMPARTMENT TO DISCHARGE DIRECTLY TO OUTDOOR AIR WITH MINIMUM FLOW RATE OF 25L/S & MAKE-UP AIR VIA OPENINGS TO AN ADJACENT ROOM WITH A FREE AREA OF 14,000 MM². THIS EXHAUST SYSTEM MUST BE INTERLOCKED WITH LIGHT SWITCH AND INCLUDE RUN-ON TIMER SO THAT THE EXHAUST SYSTEM CONTINUES TO OPERATE FOR 10 MINUTES AFTER THE LIGHT SWITCH IS OFF.
- ANY INSTALLED - KITCHEN RANGEHOOD EXHAUST TO DISCHARGE DIRECTLY OR VIA DUCT TO OUTDOOR AIR WITH MINIMUM FLOW RATE OF 40L/S & MAKE-UP AIR VIA OPENINGS TO AN ADJACENT ROOM WITH A FREE AREA OF 14,000 MM².
- LAUNDRY EXHAUST TO DISCHARGE DIRECTLY OR VIA DUCT TO OUTDOOR AIR WITH MINIMUM FLOW RATE OF 40L/S & MAKE-UP AIR VIA OPENINGS TO AN ADJACENT ROOM WITH A FREE AREA OF 14,000 MM².



CC ISSUE

General Notes			 THIS DRAWING IS THE EXCLUSIVE PROPERTY OF THE DEVELOPER & THE REPRODUCTION OF ANY PART WITHOUT THE PRIOR WRITTEN CONSENT OF THE DEVELOPER IS A VIOLATION OF APPLICABLE LAWS. IN NO EVENT SHALL THE DEVELOPER BE HELD LIABLE FOR SPECIAL COLLATERAL, INCIDENTAL OR CONSEQUENTIAL LIABILITY IN CONNECTION WITH THE USE OF THIS DIGITAL DATA ONCE RELEASED FROM THE DEVELOPER'S OFFICE. THIS DRAWING IS TO BE READ & UNDERSTOOD IN CONJUNCTION WITH THE STRUCTURAL, MECHANICAL, ELECTRICAL & / OR ANY OTHER CONSULTANT'S DOCUMENTATION AS MAY BE APPLICABLE TO THE PROJECT PRIOR TO THE START OF ANY WORKS AND FOR ITS DURATION.	PROJECT: Residential Building LOT 10 IN DP 263073 No.17 ADAM PLACE MACQUARIE FIELDS NSW 2564	DRAWING TITLE: GENERAL NOTES	NORTH:	LOT NO: 10	DATE: 21-07-2026	SCALE: 1 : 2	DRAWING No: CC.02A	REV: 11
1 : 2							DRAWN BY: ROHIT	CHECKED BY: RH		ISSUED BY:	
11	17-04-2026	DA ISSUE					DRAFTED BY: ROHIT	CLIENT NAME: Anila Gurung & Amodh Gurung			
REV	DATE	DESCRIPTION					BY				

TERMITE SHEET

- TERMITE SHEET EXTENDS THROUGH THE ENTIRE MASONRY LEAF AND IS VISIBLE AT THE FINISHED FACE OF THE WALL.



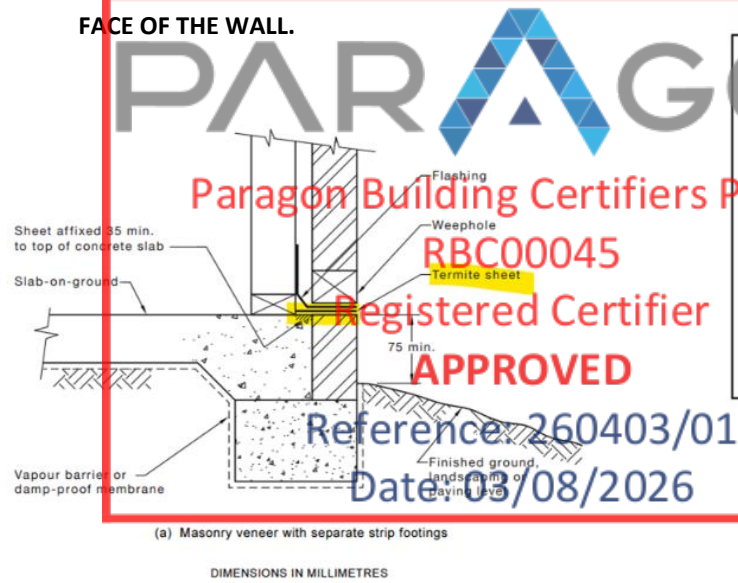


FIGURE 5.5 (in part) TYPICAL SHEET INSTALLATION TO EXTERNAL WALL WITH CONCRETE FLOOR SLAB

OVERFLOW TO BALCONY:

- SURFACE DRAIN & OVERFLOW TO BALCONY

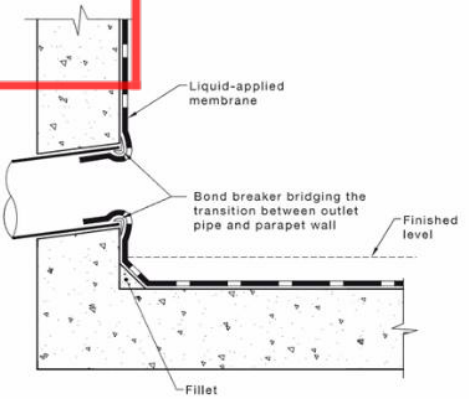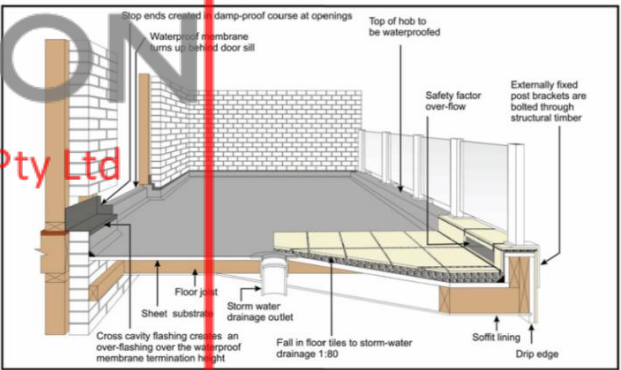

(a) Overflow through parapet

WATERPROOFING

FALL TO FLOOR WASTE TO BE MINIMUM 1:80 TO MAXIMUM 1:50

Figure 10.2.29: Typical membrane termination at drainage outlet



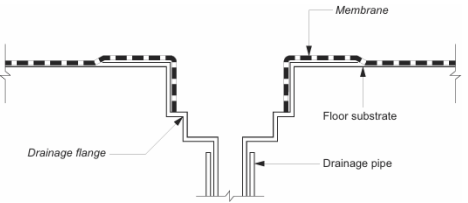


Figure 10.2.24: Typical bathroom door details for whole bathroom waterproofing

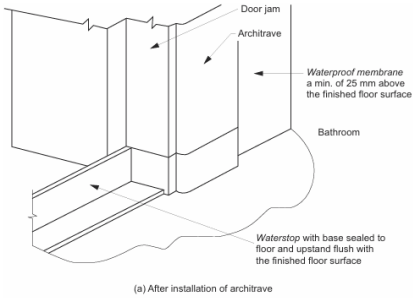


(a) After installation of architrave

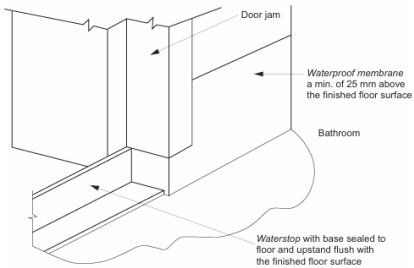


(b) Prior to installation of architrave

ENCLOSED SHOWER AREA

Figure 10.2.17: Typical hobless construction

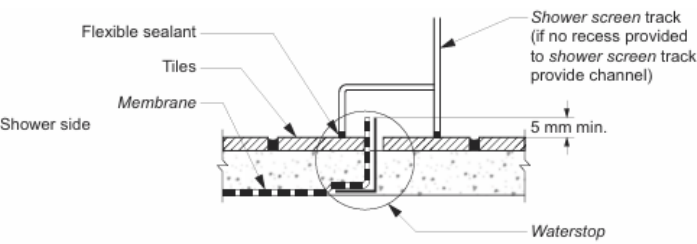


Extent of treatment for shower areas — concrete compressed fibre-cement and fibre-cement sheet floors

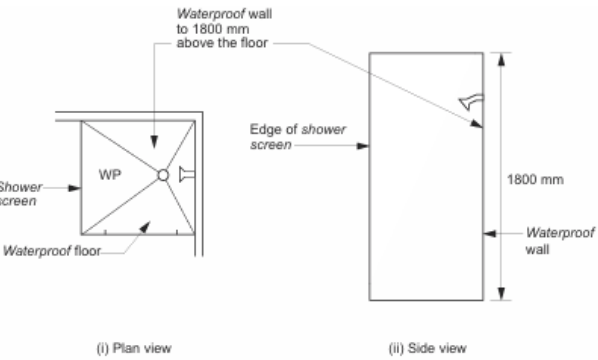

(a) Enclosed shower

DPC FOR BRICKS

DAMP-PROOF COURSE (DPC) TO EXTENDS THROUGH THE ENTIRE MASONRY LEAF AND NEED TO BE VISIBLE AT THE FINISHED FACE OF THE WALL FROM OUTSIDE

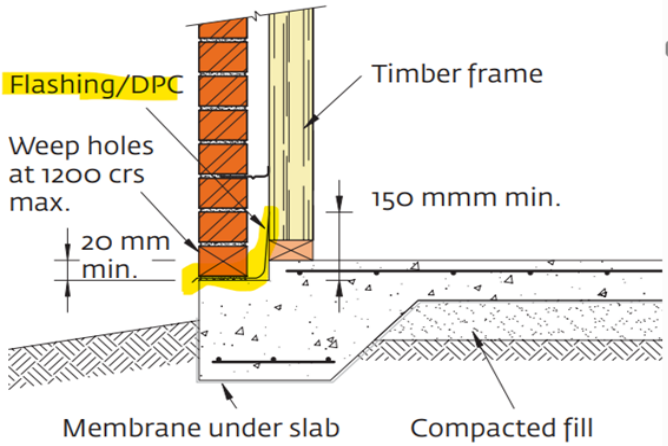


DEMOLITION


- AS 2601-2001 – DEMOLITION WORK

BASIN & BATHTUB:

Figure 10.2.5: Bath and vessel abutting wall — areas to be protected

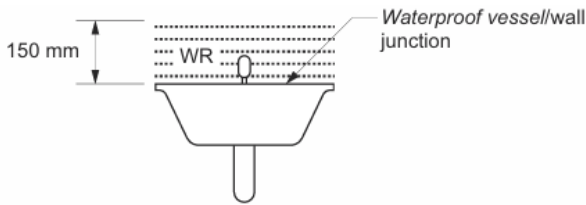

(a) Vessel abutting wall

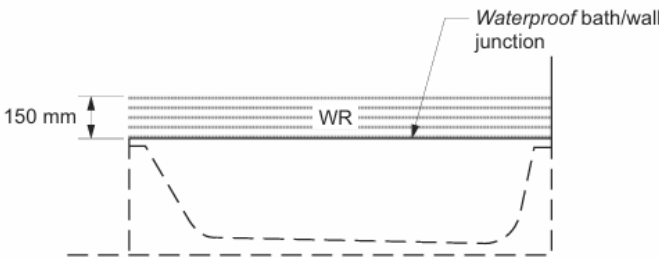

(b) Wall/bath junction

REV	DATE	DESCRIPTION	BY
11	17-04-2026	DA ISSUE	



RUBY
HOMES

THIS DRAWING IS THE EXCLUSIVE PROPERTY OF THE DEVELOPER & THE REPRODUCTION OF ANY PART WITHOUT THE PRIOR WRITTEN CONSENT OF THE DEVELOPER IS A VIOLATION OF APPLICABLE LAWS. IN NO EVENT SHALL THE DEVELOPER BE HELD LIABLE FOR SPECIAL COLLATERAL, INCIDENTAL OR CONSEQUENTIAL LIABILITY IN CONNECTION WITH THE USE OF THIS DIGITAL DATA ONCE RELEASED FROM THE DEVELOPER'S OFFICE. THIS DRAWING IS TO BE READ & UNDERSTOOD IN CONJUNCTION WITH THE STRUCTURAL, MECHANICAL, ELECTRICAL & / OR ANY OTHER CONSULTANT'S DOCUMENTATION AS MAY BE APPLICABLE TO THE PROJECT PRIOR TO THE START OF ANY WORKS AND FOR ITS DURATION.


PROJECT:
Residential Building
LOT 10 IN DP 263073
No.17 ADAM PLACE MACQUARIE
FIELDS NSW 2564

DRAWING TITLE:
GENERAL NOTES B

NORTH:


LOT NO: 10	DATE: 21-07-2026	SCALE: 1 : 2	DRAWING No: CC.02B	REV: 11
DRAWN BY: ROHIT	CHECKED BY: RH			ISSUED BY:
DRAFTED BY: ROHIT	CLIENT NAME: Anila Gurung & Amodh Gurung			

CC ISSUE

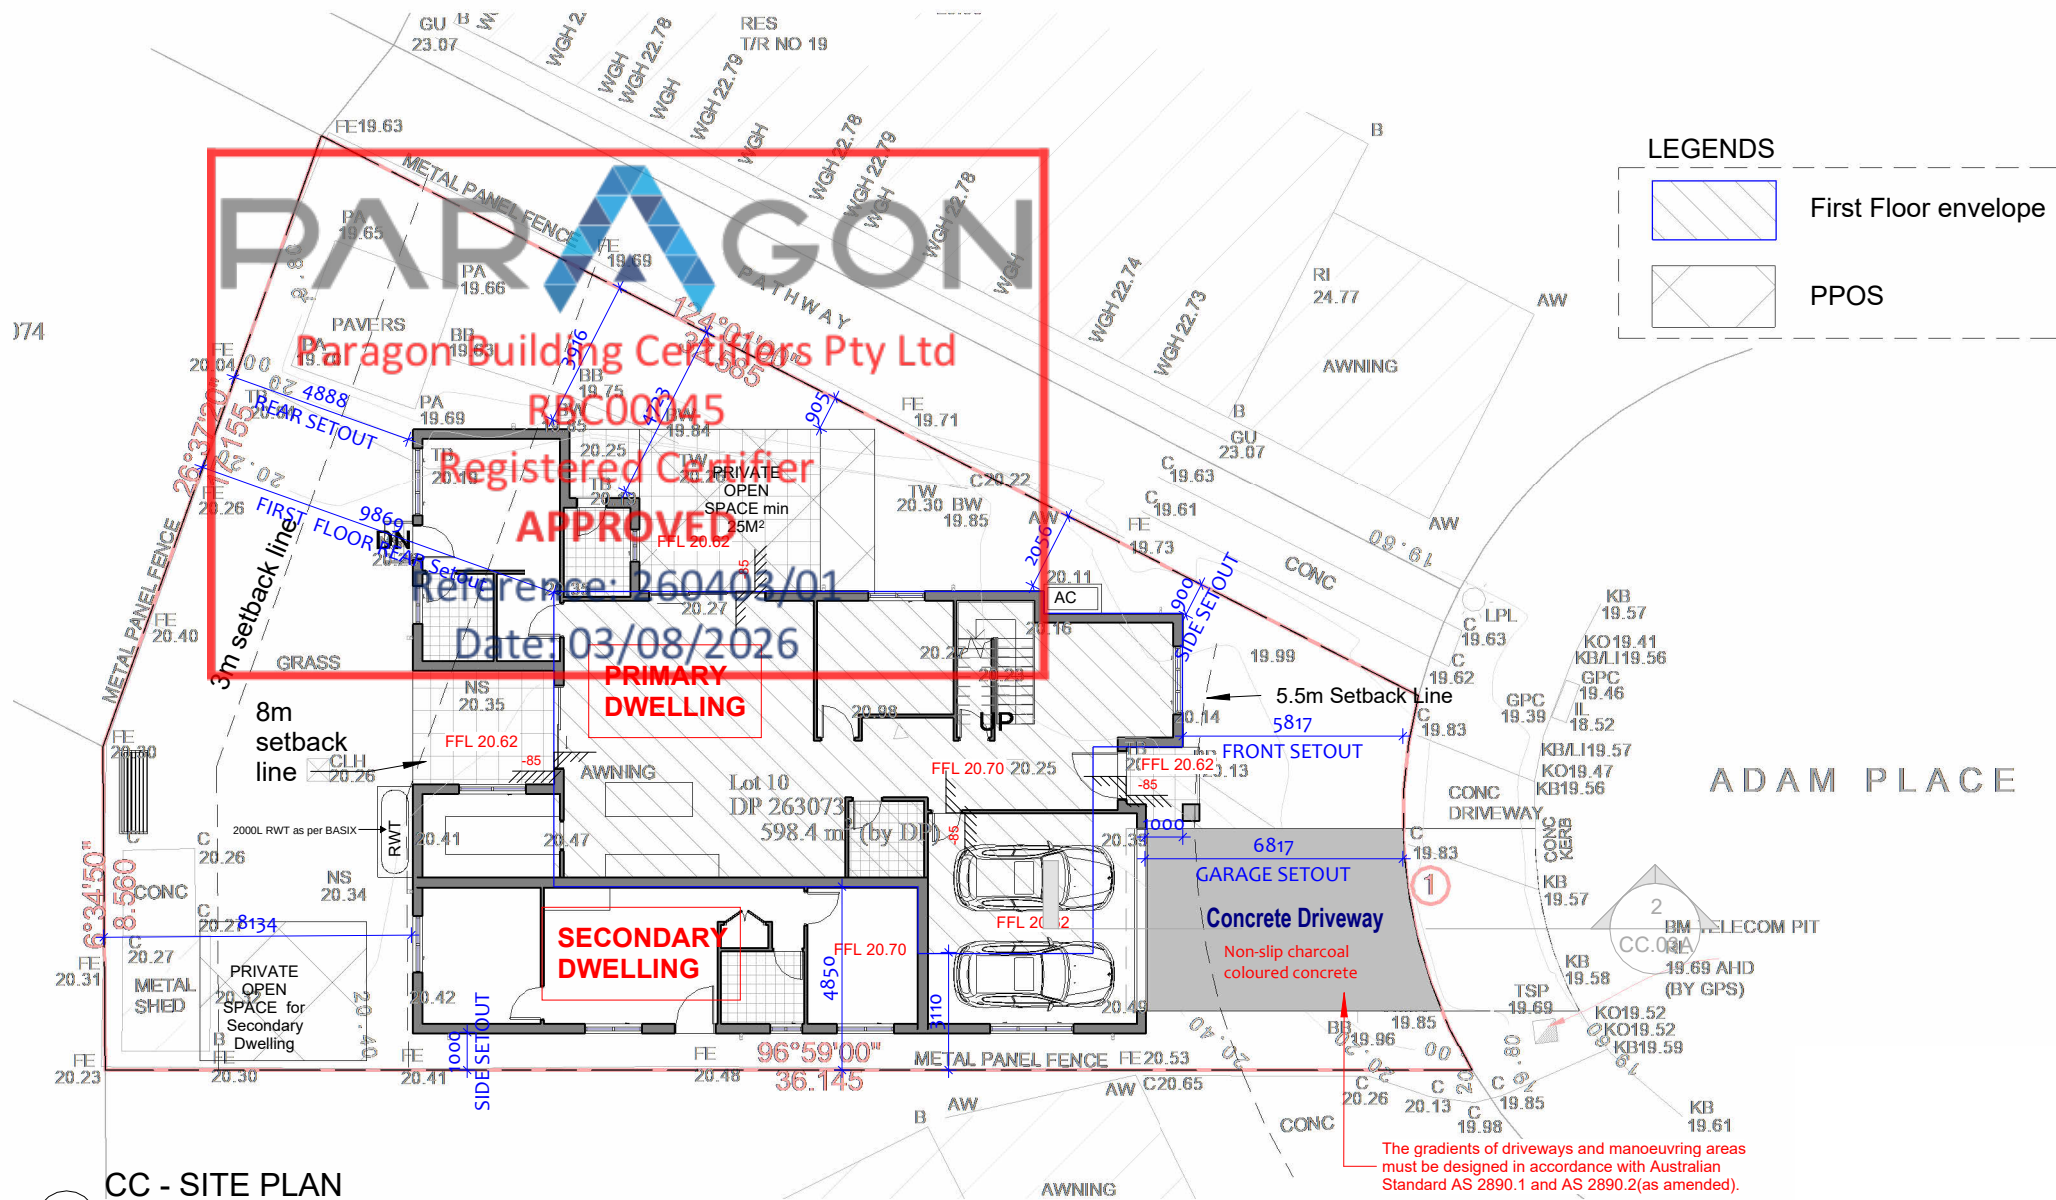

CC - SITE PLAN

1 : 200

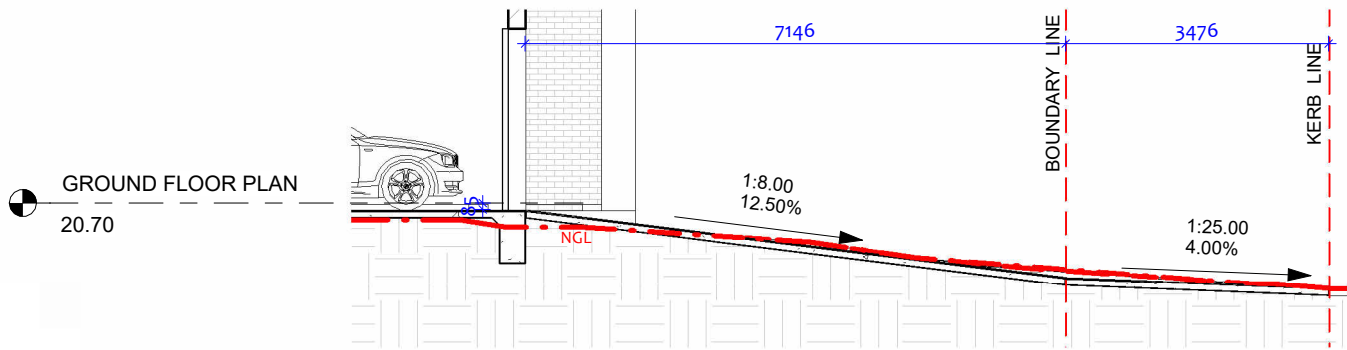

DRIVEWAY SECTION

1 : 100


REV	DATE	DESCRIPTION	BY
11	17-04-2026	DA ISSUE	



THIS DRAWING IS THE EXCLUSIVE PROPERTY OF THE DEVELOPER & THE REPRODUCTION OF ANY PART WITHOUT THE PRIOR WRITTEN CONSENT OF THE DEVELOPER IS A VIOLATION OF APPLICABLE LAWS. IN NO EVENT SHALL THE DEVELOPER BE HELD LIABLE FOR SPECIAL COLLATERAL, INCIDENTAL OR CONSEQUENTIAL LIABILITY IN CONNECTION WITH THE USE OF THIS DIGITAL DATA ONCE RELEASED FROM THE DEVELOPER'S OFFICE. THIS DRAWING IS TO BE READ & UNDERSTOOD IN CONJUNCTION WITH THE STRUCTURAL, MECHANICAL, ELECTRICAL & / OR ANY OTHER CONSULTANT'S DOCUMENTATION AS MAY BE APPLICABLE TO THE PROJECT PRIOR TO THE START OF ANY WORKS AND FOR ITS DURATION.


PROJECT:
Residential Building
LOT 10 IN DP 263073
No.17 ADAM PLACE MACQUARIE
FIELDS NSW 2564

DRAWING TITLE:
**LOCATION PLAN
AND SITE PLAN**

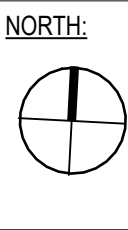

LOT NO: 10	DATE: 21-07-2026	SCALE: As indicated	DRAWING No: CC.03A	REV: 11
DRAWN BY: ROHIT	CHECKED BY: RH			ISSUED BY:
DRAFTED BY: ROHIT	CLIENT NAME: Anila Gurung & Amodh Gurung			

CC ISSUE

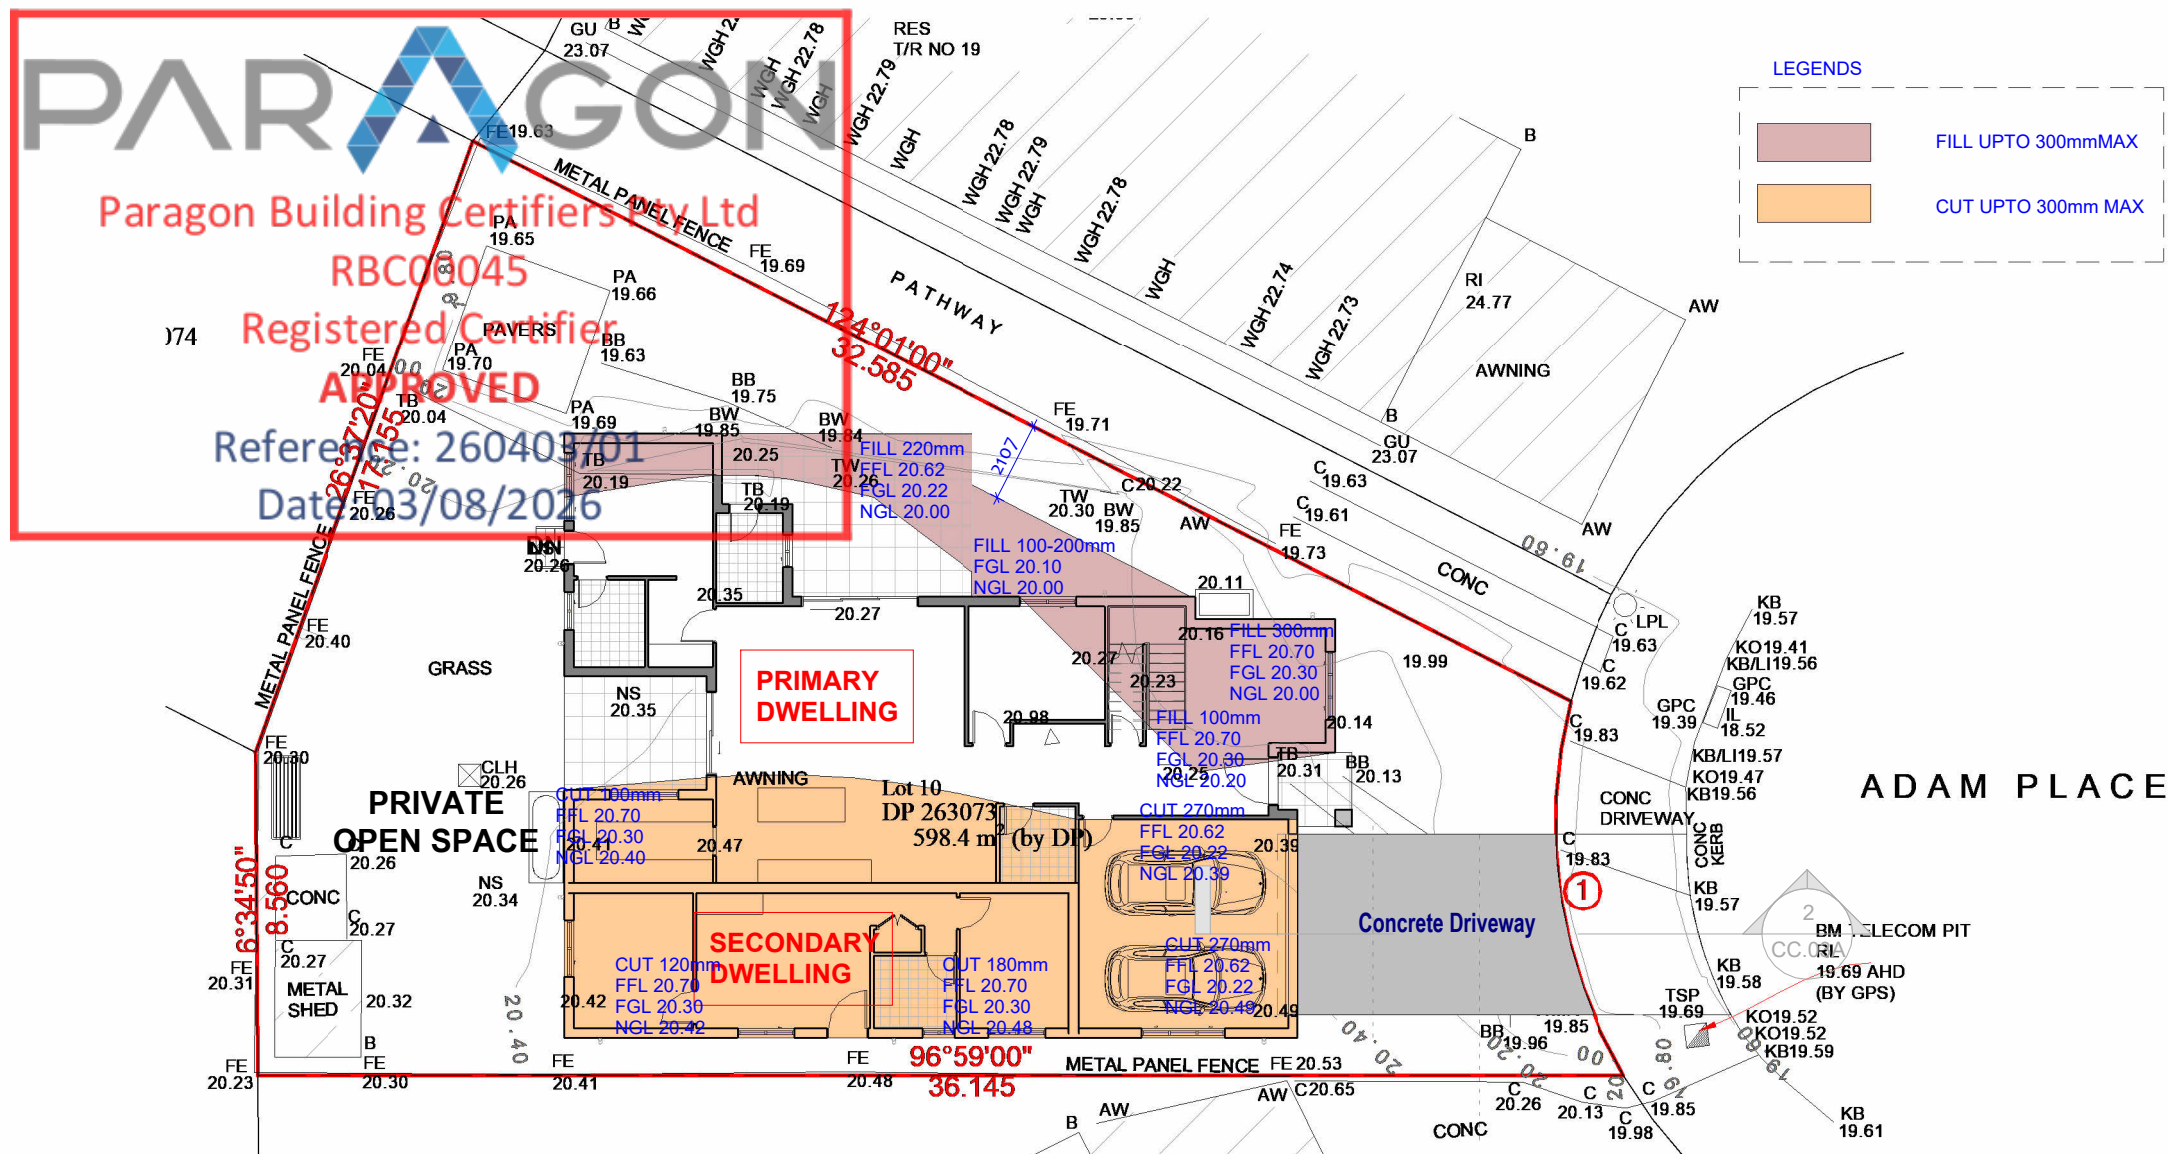

REV	DATE	DESCRIPTION	BY
11	17-04-2026	DA ISSUE	

RUBY HOMES


THIS DRAWING IS THE EXCLUSIVE PROPERTY OF THE DEVELOPER & THE REPRODUCTION OF ANY PART WITHOUT THE PRIOR WRITTEN CONSENT OF THE DEVELOPER IS A VIOLATION OF APPLICABLE LAWS. IN NO EVENT SHALL THE DEVELOPER BE HELD LIABLE FOR SPECIAL COLLATERAL, INCIDENTAL OR CONSEQUENTIAL LIABILITY IN CONNECTION WITH THE USE OF THIS DIGITAL DATA ONCE RELEASED FROM THE DEVELOPER'S OFFICE. THIS DRAWING IS TO BE READ & UNDERSTOOD IN CONJUNCTION WITH THE STRUCTURAL, MECHANICAL, ELECTRICAL & / OR ANY OTHER CONSULTANT'S DOCUMENTATION AS MAY BE APPLICABLE TO THE PROJECT PRIOR TO THE START OF ANY WORKS AND FOR ITS DURATION.

PROJECT:
Residential Building
LOT 10 IN DP 263073
No.17 ADAM PLACE MACQUARIE
FIELDS NSW 2564

DRAWING TITLE:
SITE CUT/FILL
PLAN





NORTH:

LOT NO:	DATE:	SCALE:	DRAWING No:	REV:
10	21-07-2026	1 : 200	CC.03B	11
DRAWN BY:	CHECKED BY:			ISSUED BY:
ROHIT	RH			
DRAFTED BY:	CLIENT NAME:			
ROHIT	Anila Gurung & Amodh Gurung			

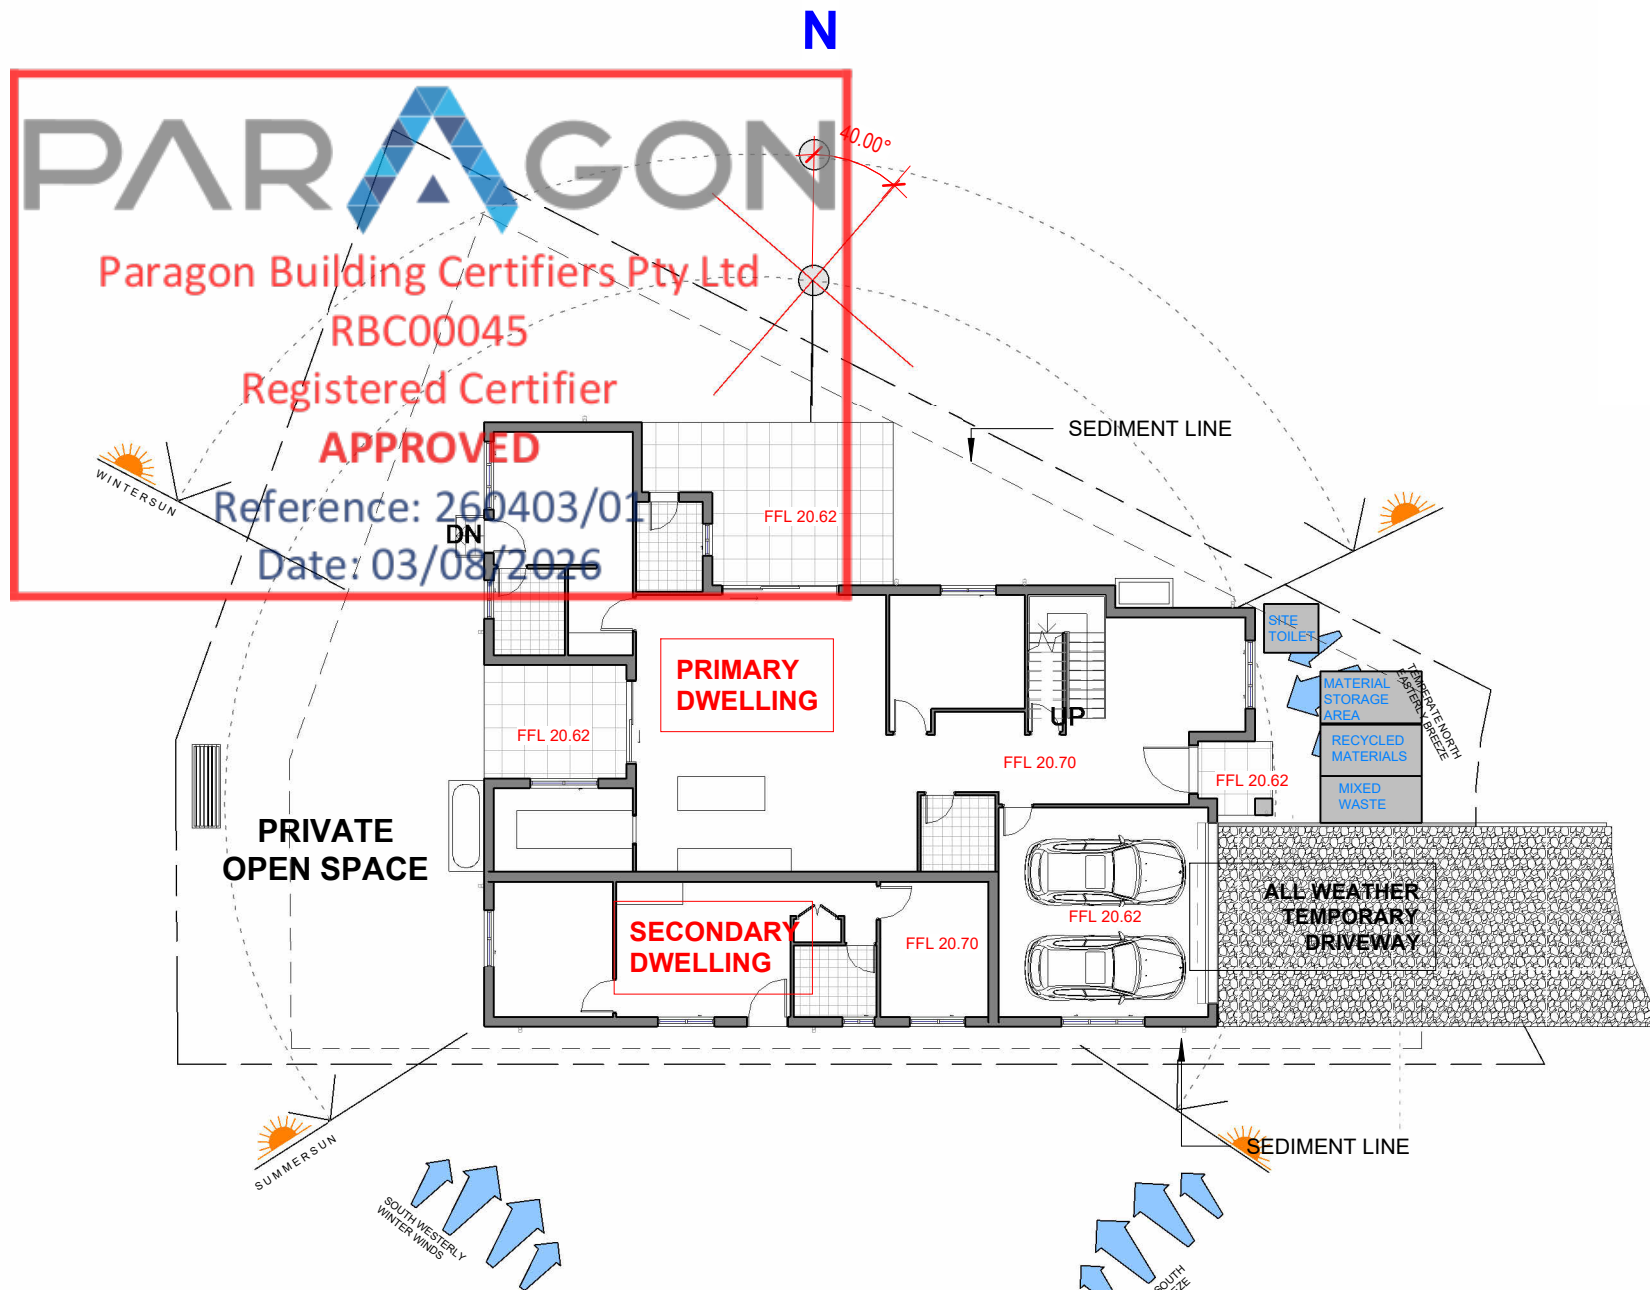

CC - SITE ANALYSIS AND SEDIMENT CONTROL PLAN

1
1 : 200

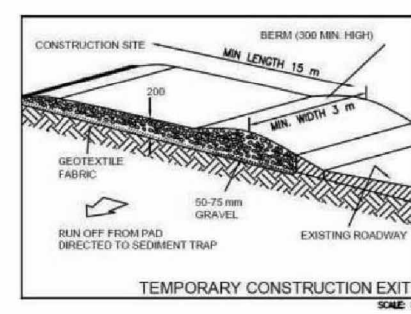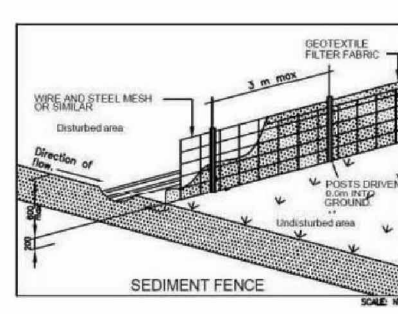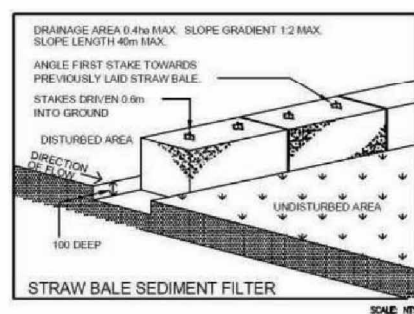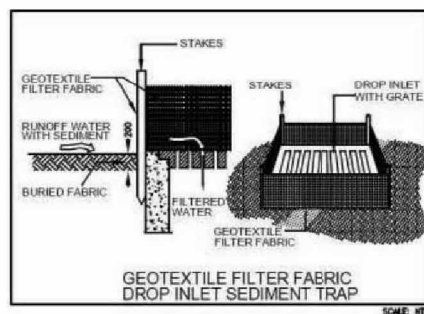

TEMPORARY 1.8M HIGH WIRE MESH FENCE WITH DUSTPROOF MESH APPLIED TO FULL HEIGHT TO BOUNDARIES AS REQUIRED

LOCATION OF WASTE BINS
SEDIMENT FENCE AS REQUIRED
GRAVEL ACCESS
SITE ACCESS AREA TO BE USED FOR WASHDOWN AREA

FOOTPATH CLEAN AND CLEAR AT ALL TIMES
LOCATION OF STOCKPILE MATERIAL
MATERIAL STORAGE AREA
TEMPORARY TOILETS
INSTALL TEMPORARY SEDIMENT BARRIERS TO ALL INLET PITS LIKELY TO COLLECT SILT LADEN WATER, TO COUNCIL'S REQUIREMENTS.

SEDIMENT AND EROSION NOTES:

- THIS PLAN TO BE READ IN CONJUNCTION WITH SEDIMENT AND EROSION CONTROL DETAILS AS ATTACHED.
- THE CONTRACTOR SHALL IMPLEMENT ALL SOIL EROSION AND SEDIMENT CONTROL MEASURES AS NECESSARY AND TO THE SATISFACTION OF COUNCIL PRIOR TO THE COMMENCEMENT AND DURING CONSTRUCTION. NO DISTURBANCE TO THE SITE SHALL BE PERMITTED OTHER THAN IN THE IMMEDIATE AREA OF THE WORK AND NO MATERIAL SHALL BE REMOVED FROM THE SITE WITHOUT COUNCIL'S APPROVAL. ALL SEDIMENT AND EROSION CONTROL DEVICES TO BE INSTALLED AND MAINTAINED IN ACCORDANCE WITH STANDARDS OUTLINED IN NSW DEPARTMENT OF HOUSING "MANAGING URBAN STORMWATER-SOILS AND CONSTRUCTIONS".
- TOPSOIL SHALL BE STRIPPED AND STOCKPILED OUTSIDE HAZARD AREAS SUCH AS DRAINAGE LINES. THIS TOP SOIL IS TO BE RESPIRED LATER ON AREAS TO BE REVEGETATED AND STABILISED ONLY. (I.E ALL FOOTPATHS, BATTERS, SITE REGARDING AREAS, BASINS AND CATCH DRAINS). TOPSOIL SHALL NOT BE RESPIRED ON ANY OTHER AREAS UNLESS SPECIALLY INSTRUCTED BY THE SUPERIDENT. IF THEY ARE TO REMAIN FOR LONGER THAN ONE MONTH STOCKPILES SHALL BE PROTECTED FROM EROSION BY COVERING THEM WITH A MULCH AND HYDROSEEDING AND, IF NECESSARY, BY LOCATING BANKS OR DRAINS DOWNSTREAM OF A STOCKPILE TO RETARD SILT LADEN RUNOFF.
- THE CONTRACTOR SHALL REGULARLY MAINTAIN ALL SEDIMENT AND EROSION CONTROL DEVICES AND REMOVE ACCUMULATED SILT FROM SUCH DEVICES SUCH THAT MORE THAN 80% OF THEIR CAPACITY LOST ALL THE SILTS TO BE PLACED OUTSIDE THE LIMIT OF WORKS. THE PERIOD FOR MAINTAINING THESE DEVICES SHALL BE AT LEAST UNTIL ALL DISTURBED AREAS ARE REVEGETATED AND FURTHER AS MAY BE DIRECTED BY THE SUPERINTENDENT OR COUNCIL.
- LAY TURF STRIP (MIN 300 mm WIDE) ON 100 mm TOPSOIL WITH 1.0 m LONG RETURNS EVERY 6.0m BEHIND ALL KERB AT THE TOP OF ALL BATTERS AND AROUND STRUCTURES IMMEDIATELY AFTER BACKFILLING OR FORMATION.
- THE CONTRACTOR SHALL GRASS SEED ALL DISTURBED AREAS WITH AN APPROVED MIX AS SHOWN AS PRACTICABLE AFTER COMPLETION OF EARTHWORKS AND REGRADING.
- VEHICULAR TRAFFIC SHALL BE CONTROLLED DURING CONSTRUCTION CONFINING ACCESS WHERE POSSIBLE TO NOMINATED STABILISED ACCESS POINTS.
- WHEN ANY DEVICES ARE TO BE HANDED OVER TO COUNCIL, THEY SHALL BE IN CLEAN AND STABLE CONDITION.
- THE CONTRACTOR SHALL IMPLEMENT DUST CONTROL BY REGULAR WETTING DOWN (BUT NOT SATURATING) DISTURBED AREA.
- PROVIDE AND MAINTAIN SILT TRAPS AROUND ALL SURFACE INLET PITS UNTIL CATCHMENT IS REVEGETATED OR PAVED.
- REVEGETATE ALL TRENCHES IMMEDIATELY UPON COMPLETION OF BACKFILLING.
- ALL DRAINAGE PIPE INLETS TO BE CAPPED UNTIL:
 - A) DOWNPIPES CONNECTED
 - B) PITS CONSTRUCTED & PROTECTED WITH SILT BARRIER

SITE WORKS NOTES

- ORIGIN OF LEVELS PROVIDED BY SURVEYOR
- THE BUILDER SHALL VERIFY ALL DIMENSIONS AND EXISTING LEVELS ON SITE PRIOR TO THE COMMENCEMENT OF WORK AND ANY DISCREPANCIES SHALL BE REPORTED TO THE SURVEYOR / ENGINEER.
- TOPSOIL SHALL BE STRIPPED FROM THE CONSTRUCTION AREA AND STOCKPILED ON SITE, TO BE LATER SPREAD OR DISPOSED OFF SITE AS DIRECTED BY SUPERVISOR / ENGINEER.
- ALL TRENCH BACKFILL MATERIAL SHALL BE COMPACTED TO THE SAME DENSITY AS THE ADJACENT MATERIAL.
- ALL SERVICE TRENCHES UNDER VEHICULAR PAVEMENTS SHALL BE BACKFILLED WITH SAND OR APPROVED GRANULAR MATERIALS, TO THE UNDERSIDE OF THE PAVEMENT, AND COMPACTED TO 98% STANDARD MAXIMUM DRY DENSITY, IN ACCORDANCE WITH AS 1289E1.1.

SD 6-9 GEOTEXTILE INLET FILTER

- FABRICATE A SEDIMENT BARRIER MADE FROM GEOTEXTILE. REFER SD6-7 FOR DETAILS.
- SUPPORT GEOTEXTILE WITH MESH TIED TO POSTS AT 1 m Ctrs.
- DO NOT COVER INLET WITH GEOTEXTILE.

SD 5-7 STABILISED SITE ACCESS

- STRIP TOPSOIL AND LEVEL SITE.
- COMPACT SUBGRADE.
- COVER AREA WITH GEOTEXTILE.
- CONSTRUCT 200 mm THICK PAD OVER GEOTEXTILE USING ROADBASE OR 30 mm AGGREGATE. Min 15 m LONG OR TO BUILDING ALIGNMENT. Min 3 m WIDE.
- CONSTRUCT HUMPS IMMEDIATELY WITHIN BOUNDARY TO DIVERT WATER TO A SEDIMENT FENCE OR OTHER SEDIMENT TRAP.

CC ISSUE

REV	DATE	DESCRIPTION	BY
11	17-04-2026	DA ISSUE	



THIS DRAWING IS THE EXCLUSIVE PROPERTY OF THE DEVELOPER & THE REPRODUCTION OF ANY PART WITHOUT THE PRIOR WRITTEN CONSENT OF THE DEVELOPER IS A VIOLATION OF APPLICABLE LAWS. IN NO EVENT SHALL THE DEVELOPER BE HELD LIABLE FOR SPECIAL COLLATERAL, INCIDENTAL OR CONSEQUENTIAL LIABILITY IN CONNECTION WITH THE USE OF THIS DIGITAL DATA ONCE RELEASED FROM THE DEVELOPER'S OFFICE. THIS DRAWING IS TO BE READ & UNDERSTOOD IN CONJUNCTION WITH THE STRUCTURAL, MECHANICAL, ELECTRICAL & / OR ANY OTHER CONSULTANT'S DOCUMENTATION AS MAY BE APPLICABLE TO THE PROJECT PRIOR TO THE START OF ANY WORKS AND FOR ITS DURATION.

PROJECT:
Residential Building
LOT 10 IN DP 263073
No.17 ADAM PLACE MACQUARIE
FIELDS NSW 2564

DRAWING TITLE:
**SITE ANALYSIS
AND SEDIMENT
CONTROL**

NORTH:


LOT NO: 10	DATE: 21-07-2026	SCALE: As indicated	DRAWING No: CC.04	REV: 11
DRAWN BY: ROHIT	CHECKED BY: RH			ISSUED BY:
DRAFTED BY: ROHIT	CLIENT NAME: Anila Gurung & Amodh Gurung			

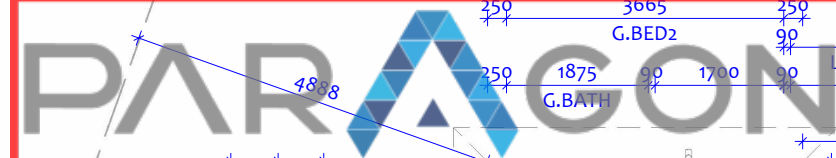

Paragon Building Certifiers Pty Ltd

RBC00045

Registered Certifier

APPROVED

Reference: 260403/01

Date: 03/08/2026

Stair to construct in accordance with NCC Part 11.2

Fall to floor waste to be minimum 1:80 to maximum 1:50. Refer below specification for waterproofing details

(Any installed) Kitchen Rangehood to comply with requirements of BCA 2022. Refer below Specifications

Smoke alarm as per AS 3786, powered from consumer mains source and interconnected.

Separating wall to achieve minimum FRL of 60/60/60 and sound insulation of 45. Refer below specification for waterproofing details

Smoke alarm as per AS 3786, powered from consumer mains source and interconnected.

Stair, Slip Resistance, Balustrade, Handrail to construct in accordance with NCC Part 11.2, 11.3, AS1170.1:2002 & AS1657:2018.


(2) Two leaves of 110 mm clay brick masonry with—
(a) a cavity not less than 50 mm between leaves; and
(b) 50 mm thick glass wool insulation with a density of 11 kg/m³ or 50 mm thick polyester insulation with a density of 20 kg/m³ in the cavity.

has an $R_w + C_p$ of not less than 50, if constructed in accordance with Figure 10.7.5a.

(3) Two leaves of 110 mm clay brick masonry with—
(a) a cavity not less than 50 mm between leaves; and
(b) 13 mm cement render on each outside face,

has an $R_w + C_p$ of not less than 50, if constructed in accordance with Figure 10.7.5b.

Figure 10.7.5a Two leaves of 110 mm clay brick masonry method 1

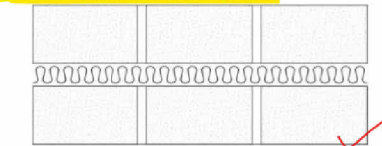

GROUND FLOOR PLAN

1

1 : 100

Waterproofing work to be as per Part 10.2 of the ABCB Housing Provisions Standard 2022

NOTE: PLEASE REFER TO TENDER FOR ALL INCLUSIONS.

CC ISSUE


REV	DATE	DESCRIPTION	BY
11	17-04-2026	DA ISSUE	

RUBY HOMES

THIS DRAWING IS THE EXCLUSIVE PROPERTY OF THE DEVELOPER & THE REPRODUCTION OF ANY PART WITHOUT THE PRIOR WRITTEN CONSENT OF THE DEVELOPER IS A VIOLATION OF APPLICABLE LAWS. IN NO EVENT SHALL THE DEVELOPER BE HELD LIABLE FOR SPECIAL COLLATERAL, INCIDENTAL OR CONSEQUENTIAL LIABILITY IN CONNECTION WITH THE USE OF THIS DIGITAL DATA ONCE RELEASED FROM THE DEVELOPER'S OFFICE. THIS DRAWING IS TO BE READ & UNDERSTOOD IN CONJUNCTION WITH THE STRUCTURAL, MECHANICAL, ELECTRICAL & / OR ANY OTHER CONSULTANT'S DOCUMENTATION AS MAY BE APPLICABLE TO THE PROJECT PRIOR TO THE START OF ANY WORKS AND FOR ITS DURATION.

PROJECT:
Residential Building
LOT 10 IN DP 263073
No.17 ADAM PLACE MACQUARIE
FIELDS NSW 2564

DRAWING TITLE:
GROUND FLOOR PLAN

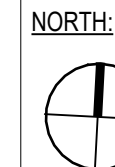

LOT NO: 10	DATE: 21-07-2026	SCALE: 1 : 100	DRAWING No: CC.05	REV: 11
DRAWN BY: AS	CHECKED BY: RH			ISSUED BY:
DRAFTED BY: ROHIT	CLIENT NAME: Anila Gurung & Amodh Gurung			

FIGURE 6.12 Typical Installation Detail for Eaves



Table 1 – Masonry thickness

Material thickness (mm)	60	90	110	130	160	180
Fire resistance period for insulation (mins)	30	60	90	120	180	240


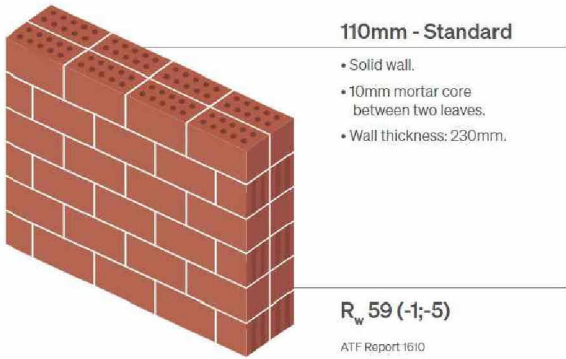


TABLE 6.02 Frame and Fastener Spacing – 6mm Cladding Sheet to Ceilings.

Maximum Frame Spacing (mm)	Wind Classification	Timber Framing Maximum Fastener Spacing (mm)	
		Edge	Field
500	N1	225	225
500	N2	175	175
400	N3/C1	150	150
300	N4/C2	125	125

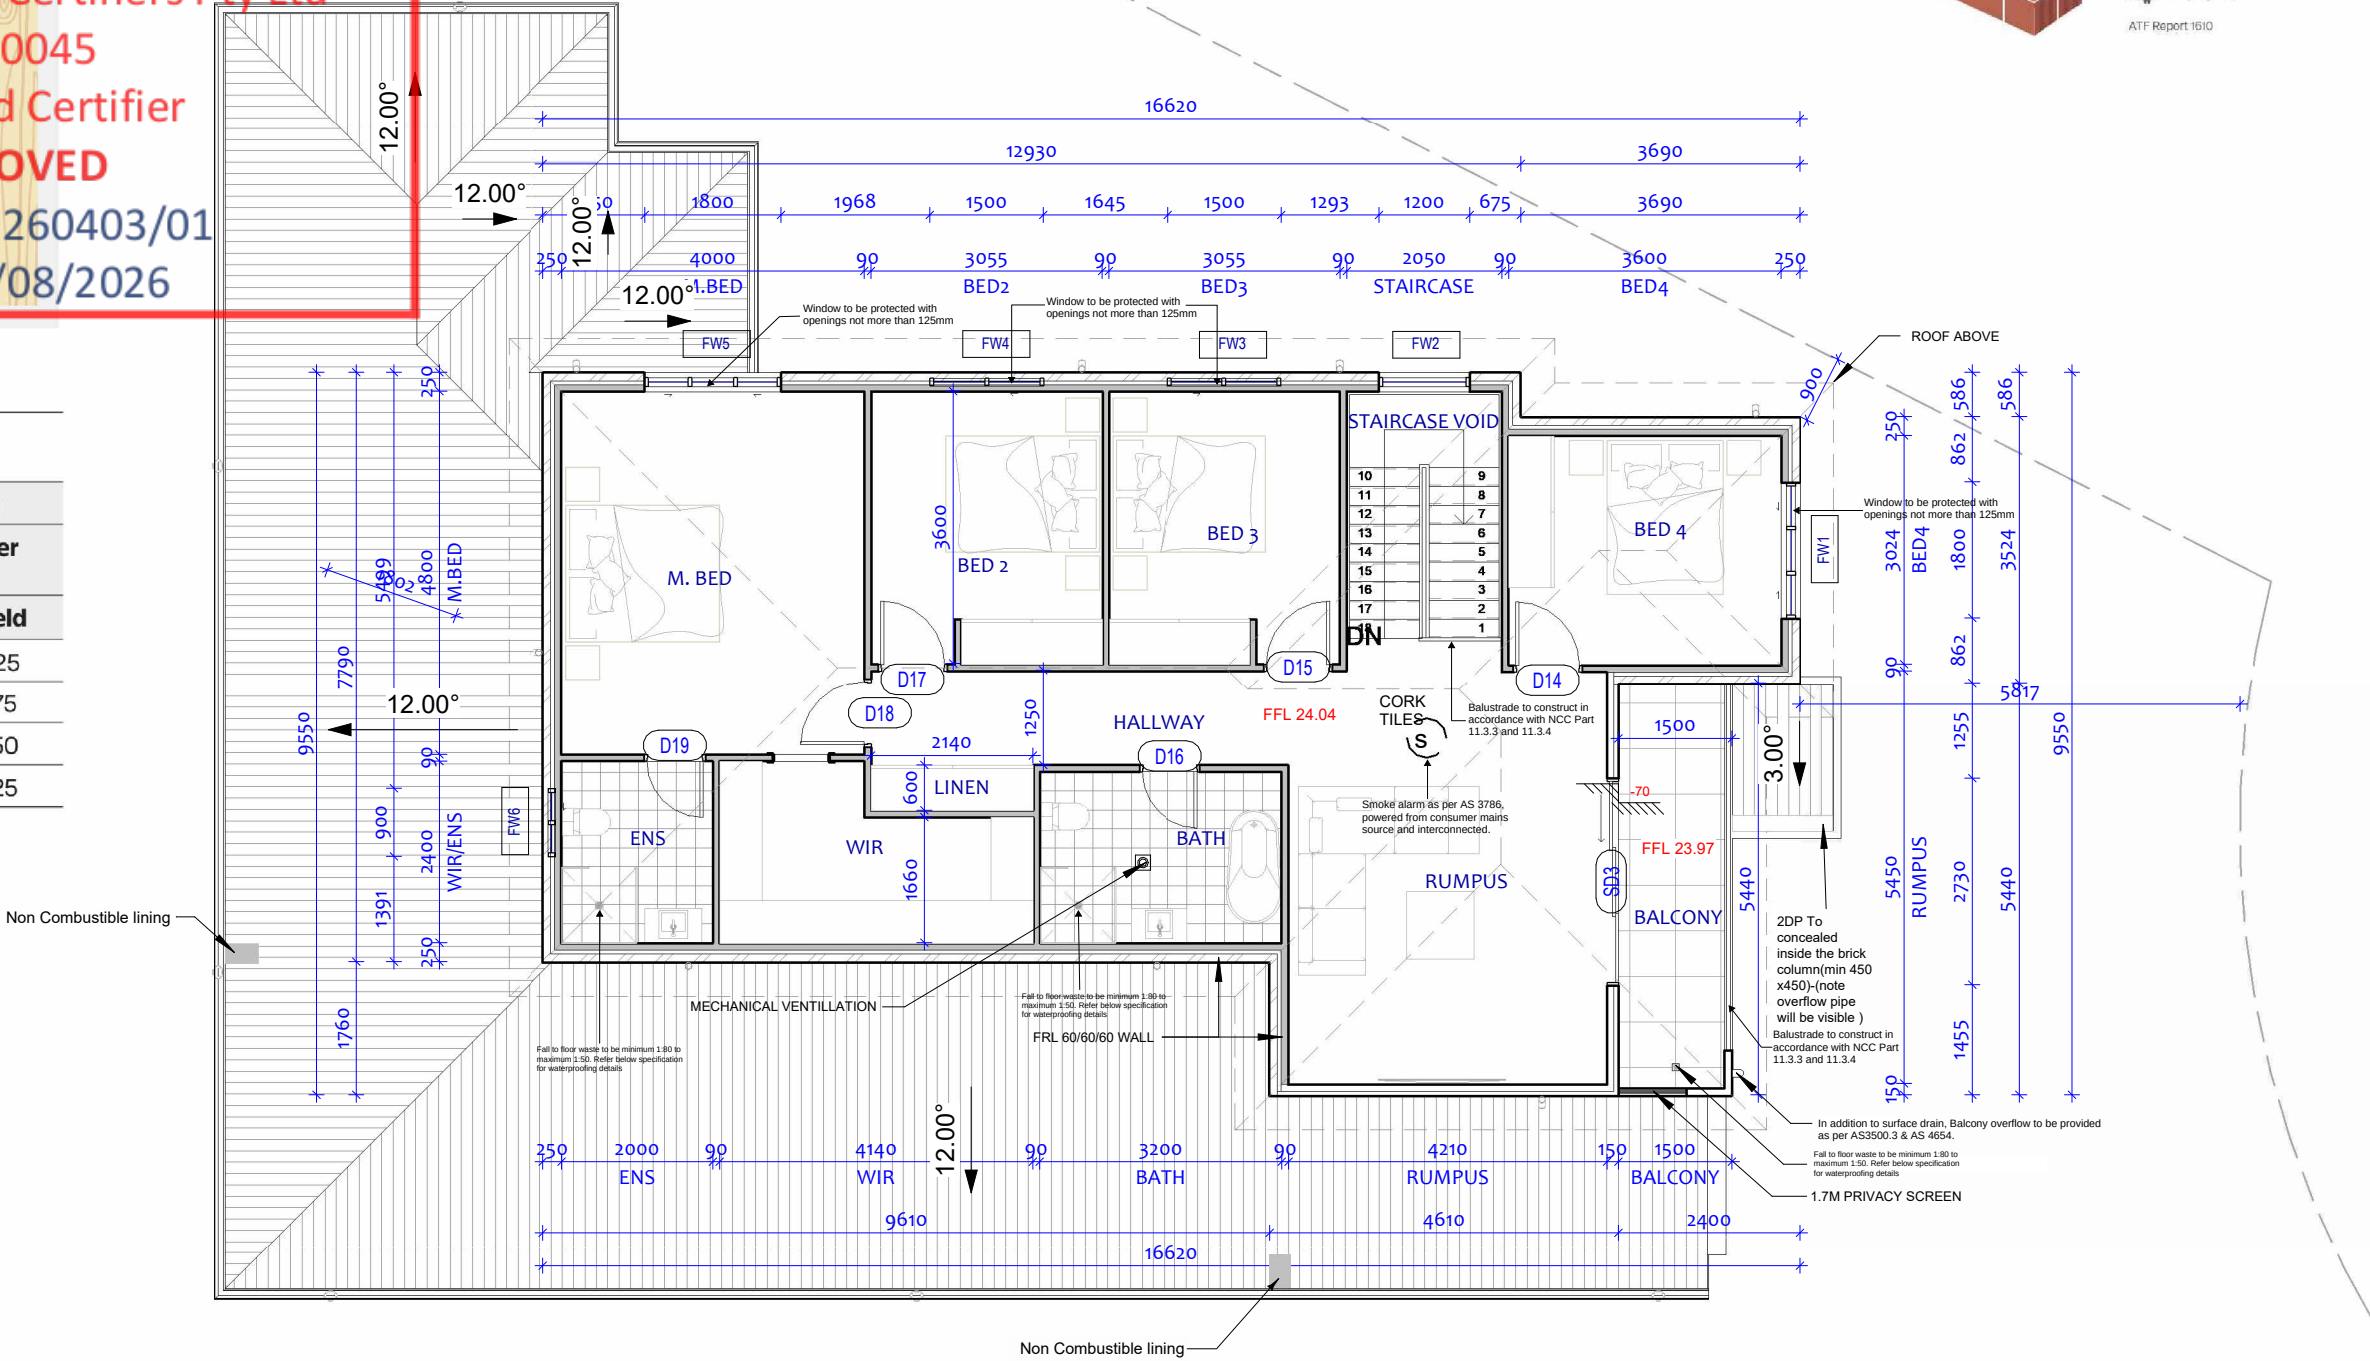

1 FIRST FLOOR PLAN
1 : 100

NOTE: PLEASE REFER TO TENDER FOR ALL INCLUSIONS.

Waterproofing work to be as per Part 10.2 of the ABCB Housing Provisions Standard 2022

CC ISSUE

REV	DATE	DESCRIPTION	BY
11	17-04-2026	DA ISSUE	

RUBY HOMES


THIS DRAWING IS THE EXCLUSIVE PROPERTY OF THE DEVELOPER & THE REPRODUCTION OF ANY PART WITHOUT THE PRIOR WRITTEN CONSENT OF THE DEVELOPER IS A VIOLATION OF APPLICABLE LAWS. IN NO EVENT SHALL THE DEVELOPER BE HELD LIABLE FOR SPECIAL COLLATERAL, INCIDENTAL OR CONSEQUENTIAL LIABILITY IN CONNECTION WITH THE USE OF THIS DIGITAL DATA ONCE RELEASED FROM THE DEVELOPER'S OFFICE. THIS DRAWING IS TO BE READ & UNDERSTOOD IN CONJUNCTION WITH THE STRUCTURAL, MECHANICAL, ELECTRICAL & / OR ANY OTHER CONSULTANT'S DOCUMENTATION AS MAY BE APPLICABLE TO THE PROJECT PRIOR TO THE START OF ANY WORKS AND FOR ITS DURATION.

PROJECT:
Residential Building
LOT 10 IN DP 263073
No.17 ADAM PLACE MACQUARIE
FIELDS NSW 2564


DRAWING TITLE:
**FIRST FLOOR
LEVEL**

NORTH:

LOT NO: 10	DATE: 21-07-2026	SCALE: 1 : 100	DRAWING No: CC.06	REV: 11
DRAWN BY: AS	CHECKED BY: RH			ISSUED BY:
DRAFTED BY: ROHIT	CLIENT NAME: Anila Gurung & Amodh Gurung			

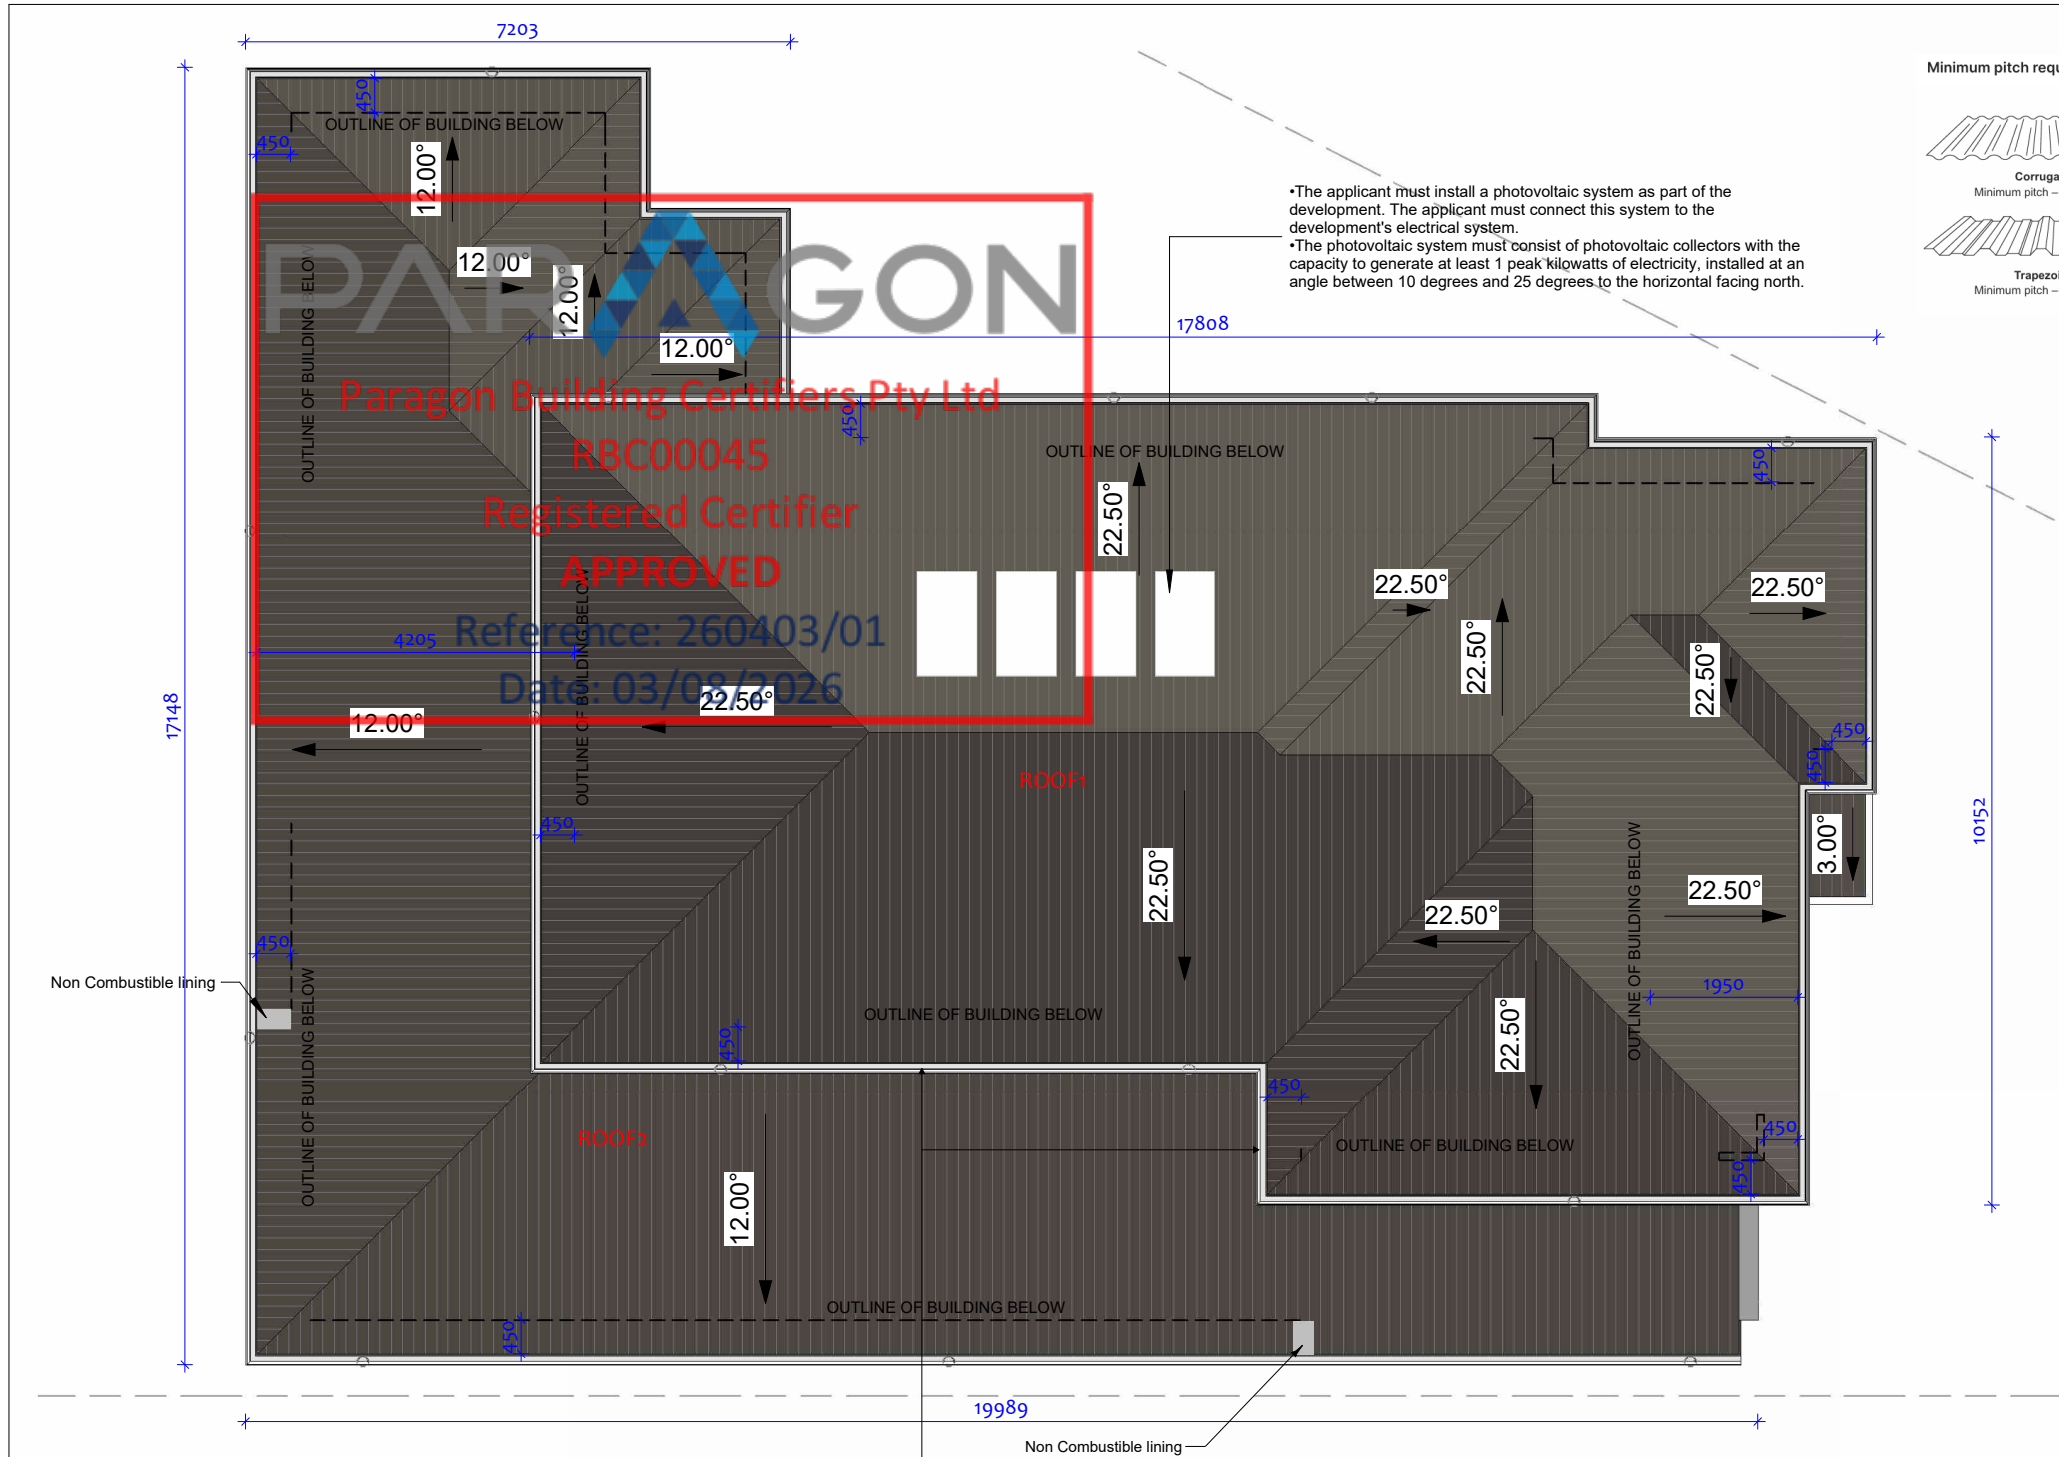

Minimum pitch requirements for metal roofing profiles

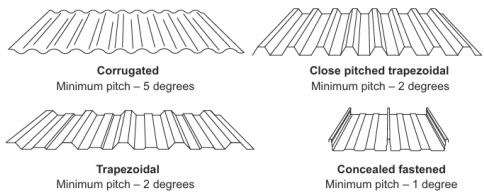

IMPORTANT NOTES:
ALL DIMENSIONS AND NOTES ON ALL PLANS MUST BE CHECKED AND VERIFIED BY BUILDERS AND OWNER PRIOR TO COMMENCEMENT OF ANY BUILDING WORKS. TO CLARIFY AND CONFIRM WITH CONSTRUCTION COMPANY FOR DISCREPANCIES ON ALL DOCUMENTS AND PLANS PROVIDED FOR CONSTRUCTION. ANY WORK INDICATED ON THE PLAN BUT NOT IN THE SPECIFICATION BUT WHICH IS NECESSARY AS PART OF THE CONTRACT, VARIATION TO PLANS, SPECIFICATIONS MAY NOT BE MADE WITHOUT THE WRITTEN CONSENT OF OWNER. IT IS THE RESPONSIBILITY OF THE BUILDER/END USER TO VERIFY PLANS AND SPECIFICATIONS AS TO THEIR ACCURACY AND COMPLY CURRENT BCA AND AUSTRALIAN STANDARDS. WINDOWS TO COMPLY WITH 3.9.3.5 OF THE BCA.

VENTILATION OF ROOF SPACES

ROOF SPACE AS PER 10.8.3 1(a) & 1(b)

(i) VENTILATED TO OUTDOOR AIR THROUGH EVENLY DISTRIBUTED OPENINGS IN ACCORDANCE WITH TABLE 10.8.3;

TABLE 10.8.3: ROOF SPACE VENTILATION REQUIREMENTS

ROOF PITCH	VENTILATION OPENINGS
< 10°	25,000 MM ² /M PROVIDED AT EACH OF TWO OPPOSING ENDS
≥ 10° AND < 15°	25,000 MM ² /M PROVIDED AT THE EAVES AND 5,000 MM ² /M AT HIGH LEVEL
≥ 15° AND < 75°	7,000 MM ² /M PROVIDED AT THE EAVES AND 5,000 MM ² /M AT HIGH LEVEL, PLUS AN ADDITIONAL 18,000 MM ² /M AT THE EAVES IF THE ROOF HAS A CATHEDRAL CEILING

Figure 10.8.3 (explanatory): Example of roof space with low level ventilation


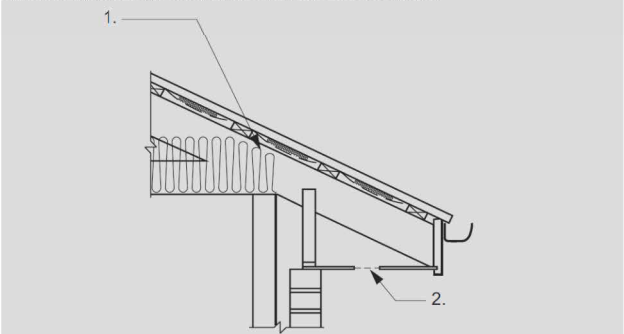


Figure Notes
(1) Minimum 20 mm gap maintained between insulation and sarking.
(2) Eave ventilation opening in accordance with Table 10.8.3.

ROOF PLAN

1

1 : 100

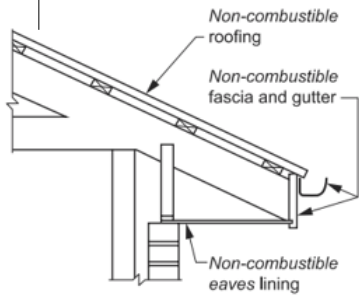

(d) Eaves construction

Roof Schedule

Mark	Base Level	Area	Comments
R3	GROUND CEILING LEVEL	3 m ²	COLORBOND ROOF
ROOF1	CEILING LEVEL	172 m ²	COLORBOND ROOF
ROOF 2	FIRST FLOOR PLAN	140 m ²	COLORBOND ROOF

Grand total: 3

315 m²

CC ISSUE

REV	DATE	DESCRIPTION	BY
11	17-04-2026	DA ISSUE	


RUBY HOMES

THIS DRAWING IS THE EXCLUSIVE PROPERTY OF THE DEVELOPER & THE REPRODUCTION OF ANY PART WITHOUT THE PRIOR WRITTEN CONSENT OF THE DEVELOPER IS A VIOLATION OF APPLICABLE LAWS. IN NO EVENT SHALL THE DEVELOPER BE HELD LIABLE FOR SPECIAL COLLATERAL, INCIDENTAL OR CONSEQUENTIAL LIABILITY IN CONNECTION WITH THE USE OF THIS DIGITAL DATA ONCE RELEASED FROM THE DEVELOPER'S OFFICE. THIS DRAWING IS TO BE READ & UNDERSTOOD IN CONJUNCTION WITH THE STRUCTURAL, MECHANICAL, ELECTRICAL & / OR ANY OTHER CONSULTANT'S DOCUMENTATION AS MAY BE APPLICABLE TO THE PROJECT PRIOR TO THE START OF ANY WORKS AND FOR ITS DURATION.



PROJECT:
Residential Building
LOT 10 IN DP 263073
No.17 ADAM PLACE MACQUARIE
FIELDS NSW 2564

DRAWING TITLE:
ROOF PLAN

NORTH:

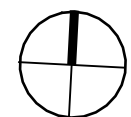

LOT NO: 10	DATE: 21-07-2026	SCALE: 1 : 100	DRAWING No: CC.07	REV: 11
DRAWN BY: AS	CHECKED BY: RH			ISSUED BY:
DRAFTED BY: ROHIT	CLIENT NAME: Anila Gurung & Amodh Gurung			

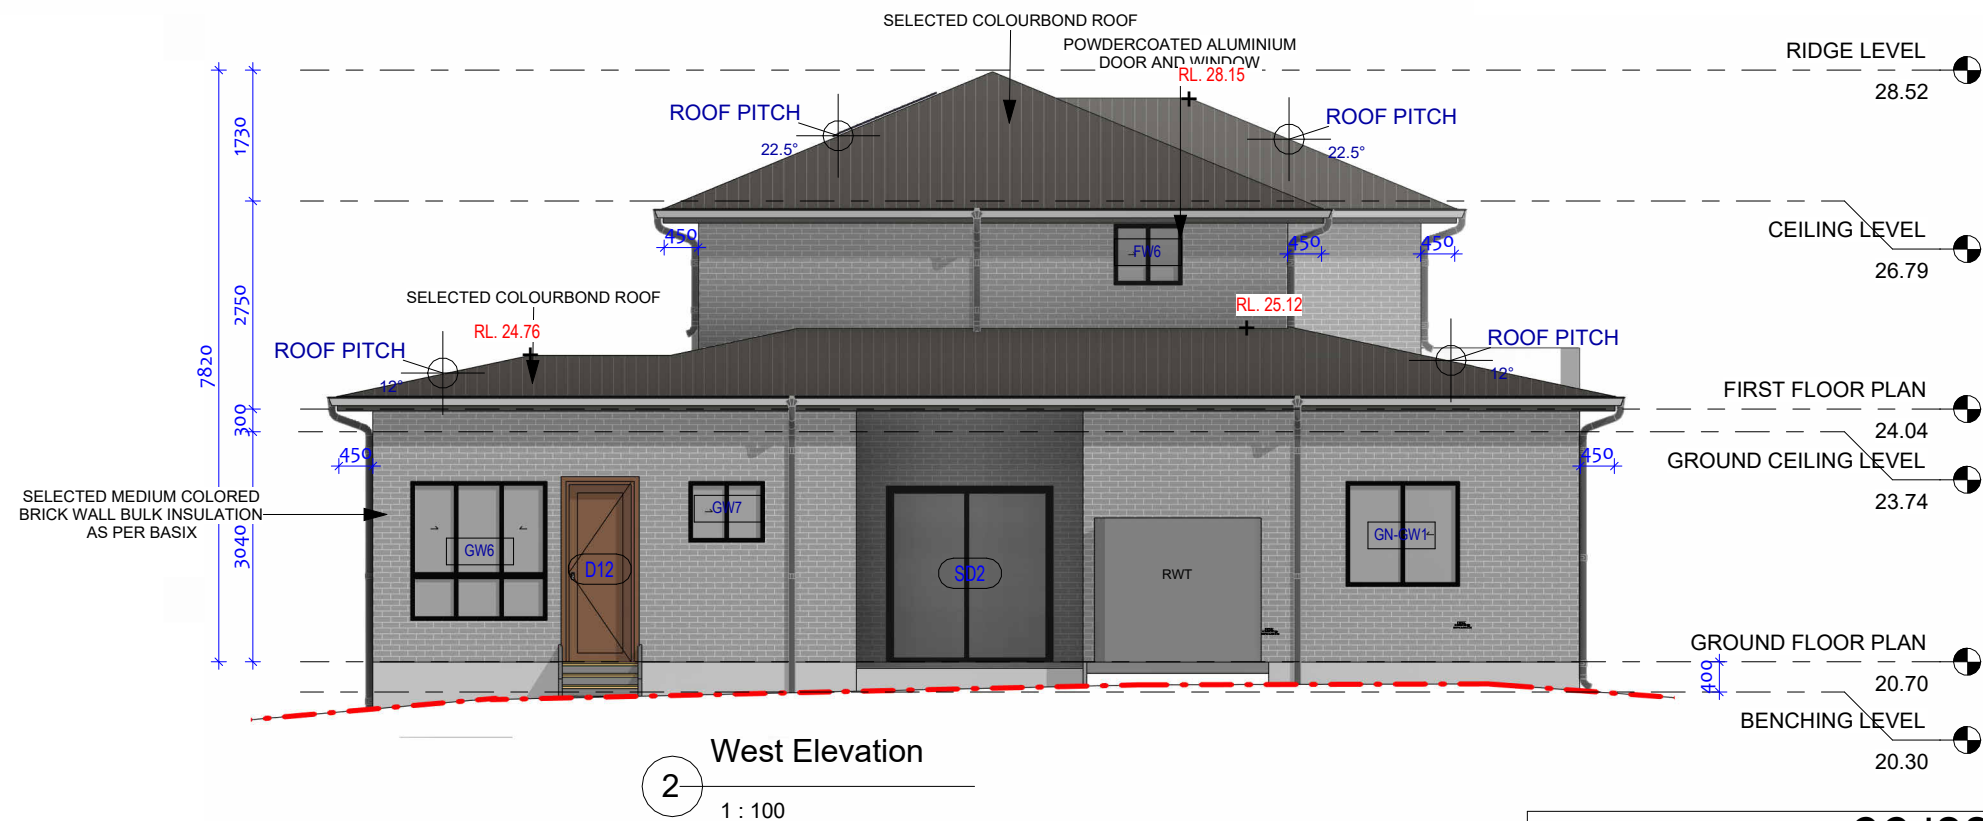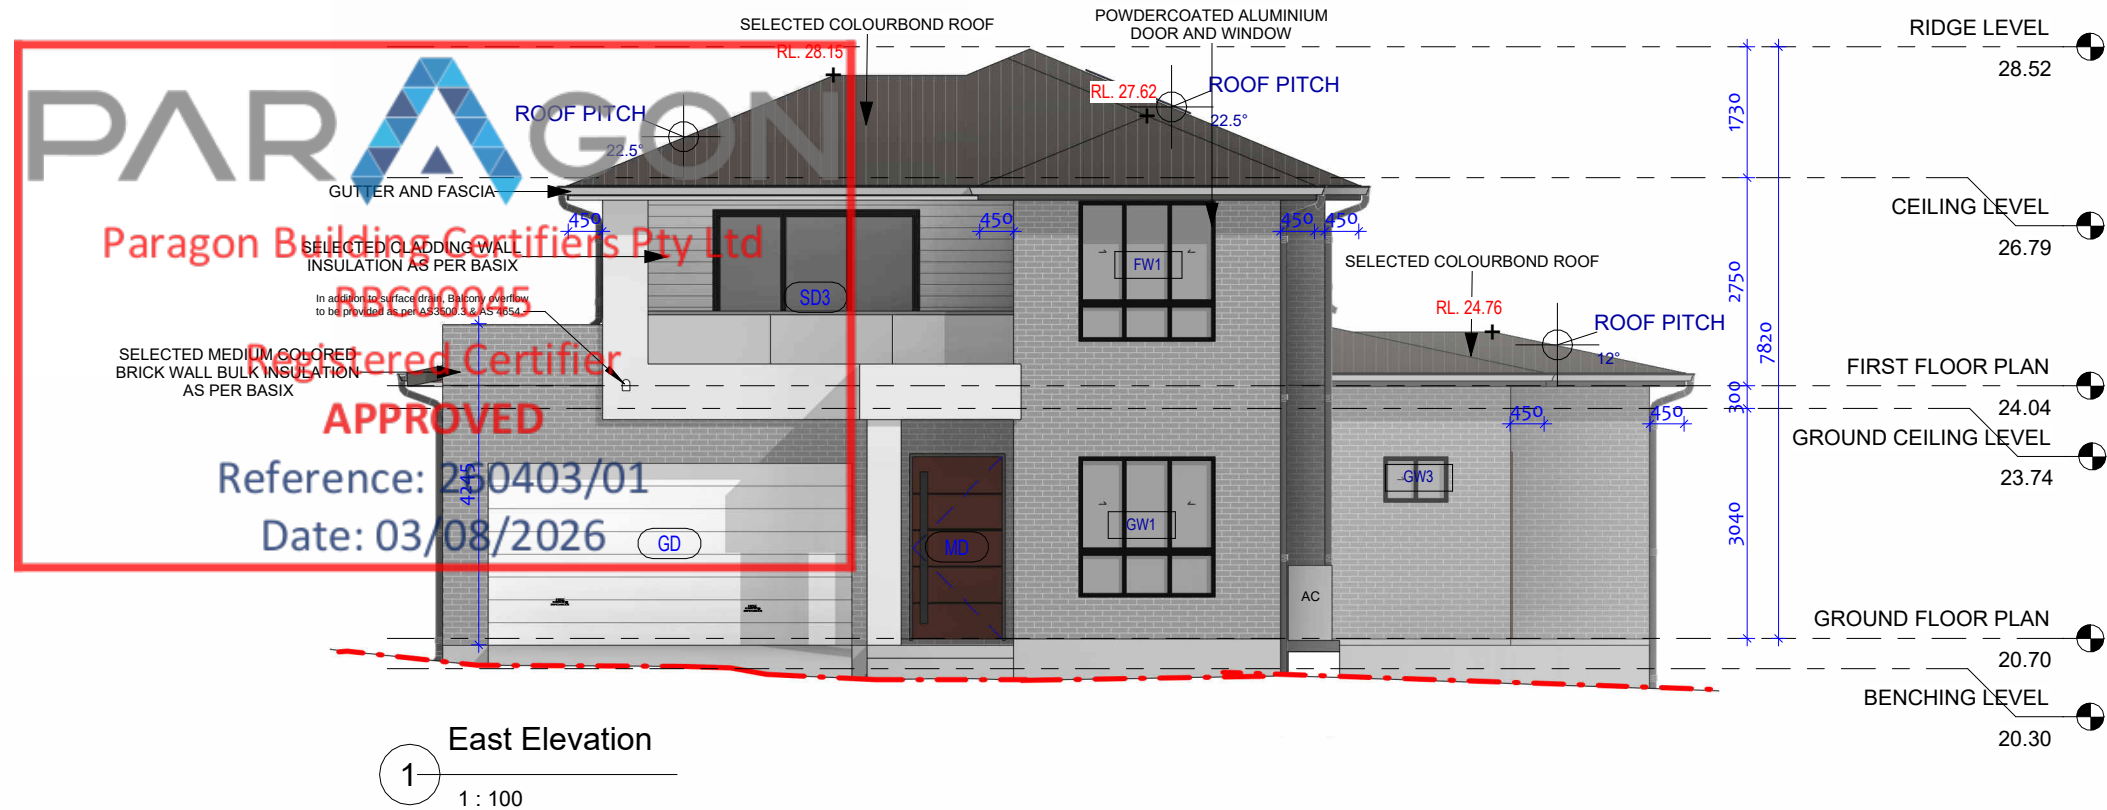

REV	DATE	DESCRIPTION	BY
11	17-04-2026	DA ISSUE	


RUBY HOMES

THIS DRAWING IS THE EXCLUSIVE PROPERTY OF THE DEVELOPER & THE REPRODUCTION OF ANY PART WITHOUT THE PRIOR WRITTEN CONSENT OF THE DEVELOPER IS A VIOLATION OF APPLICABLE LAWS. IN NO EVENT SHALL THE DEVELOPER BE HELD LIABLE FOR SPECIAL COLLATERAL, INCIDENTAL OR CONSEQUENTIAL LIABILITY IN CONNECTION WITH THE USE OF THIS DIGITAL DATA ONCE RELEASED FROM THE DEVELOPER'S OFFICE. THIS DRAWING IS TO BE READ & UNDERSTOOD IN CONJUNCTION WITH THE STRUCTURAL, MECHANICAL, ELECTRICAL & / OR ANY OTHER CONSULTANT'S DOCUMENTATION AS MAY BE APPLICABLE TO THE PROJECT PRIOR TO THE START OF ANY WORKS AND FOR ITS DURATION.

PROJECT:
Residential Building
LOT 10 IN DP 263073
No.17 ADAM PLACE MACQUARIE
FIELDS NSW 2564

DRAWING TITLE:
ELEVATION 01

NORTH:

LOT NO:
10
DRAWN BY:
ROHIT
DRAFTED BY:
ROHIT

DATE:
21-07-2026
CHECKED BY:
RH


SCALE:
1 : 100

DRAWING No:
CC.08


REV:
11
ISSUED BY:

CLIENT NAME:
Anila Gurung & Amodh Gurung

CC ISSUE

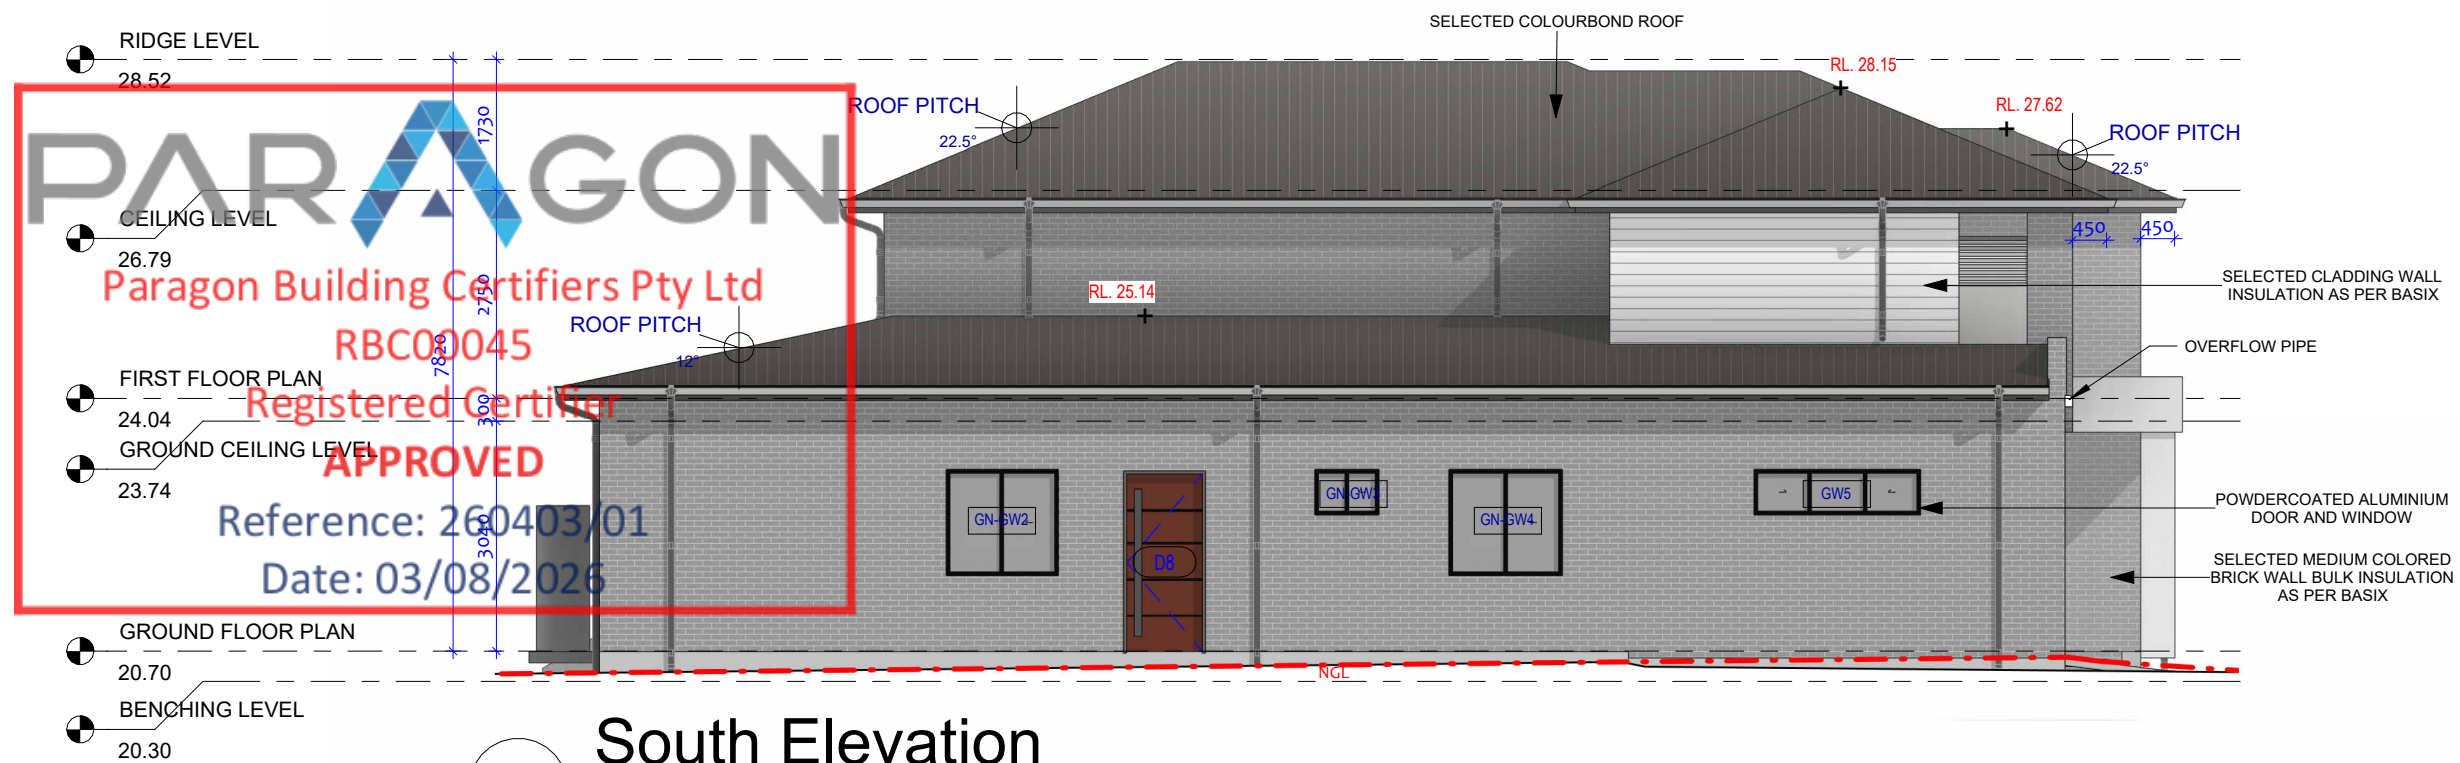

1 South Elevation
1 : 100

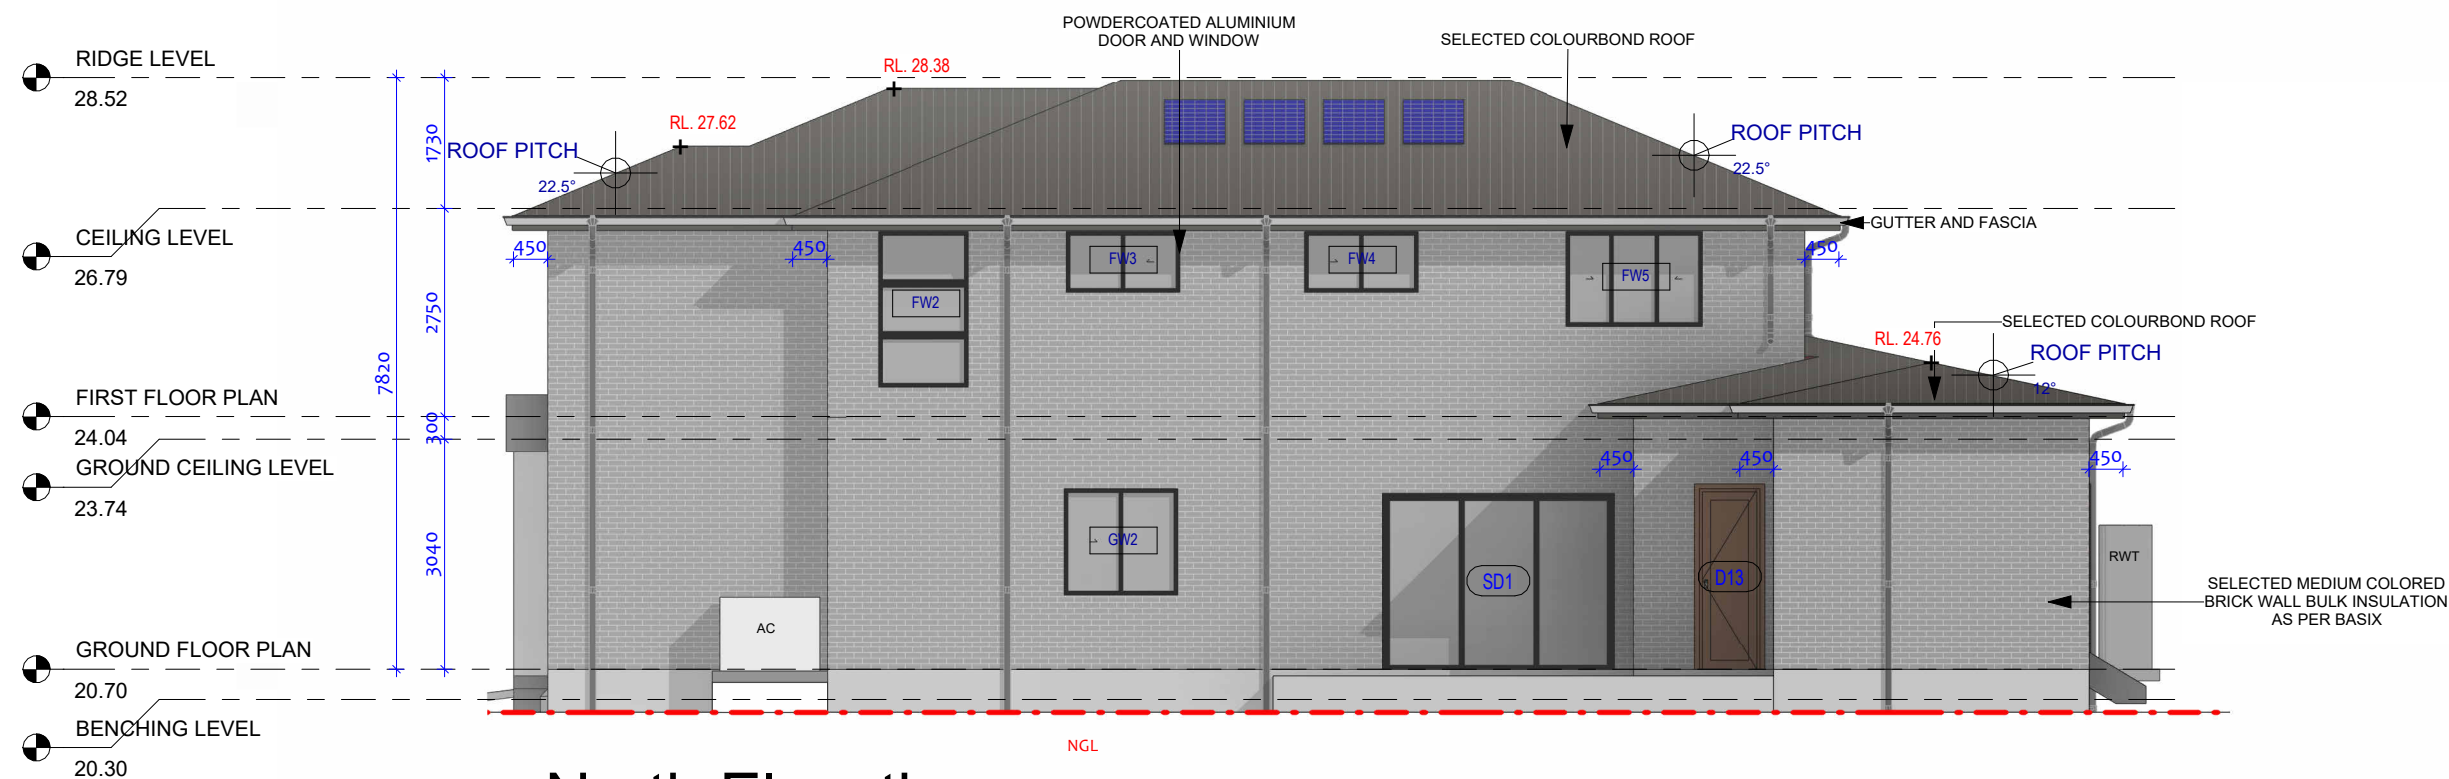

2 North Elevation
1 : 100

REV	DATE	DESCRIPTION	BY
11	17-04-2026	DA ISSUE	

RUBY HOMES

THIS DRAWING IS THE EXCLUSIVE PROPERTY OF THE DEVELOPER & THE REPRODUCTION OF ANY PART WITHOUT THE PRIOR WRITTEN CONSENT OF THE DEVELOPER IS A VIOLATION OF APPLICABLE LAWS. IN NO EVENT SHALL THE DEVELOPER BE HELD LIABLE FOR SPECIAL COLLATERAL, INCIDENTAL OR CONSEQUENTIAL LIABILITY IN CONNECTION WITH THE USE OF THIS DIGITAL DATA ONCE RELEASED FROM THE DEVELOPER'S OFFICE. THIS DRAWING IS TO BE READ & UNDERSTOOD IN CONJUNCTION WITH THE STRUCTURAL, MECHANICAL, ELECTRICAL & / OR ANY OTHER CONSULTANT'S DOCUMENTATION AS MAY BE APPLICABLE TO THE PROJECT PRIOR TO THE START OF ANY WORKS AND FOR ITS DURATION.

PROJECT:
Residential Building
LOT 10 IN DP 263073
No.17 ADAM PLACE MACQUARIE
FIELDS NSW 2564

DRAWING TITLE:
ELEVATION 02

NORTH:

LOT NO:
10
DRAWN BY:
ROHIT
DRAFTED BY:
ROHIT

DATE:
21-07-2026
CHECKED BY:
RH


SCALE:
1 : 100

DRAWING No:
CC.09


REV:
11
ISSUED BY:

CLIENT NAME:
Anila Gurung & Amodh Gurung

CC ISSUE

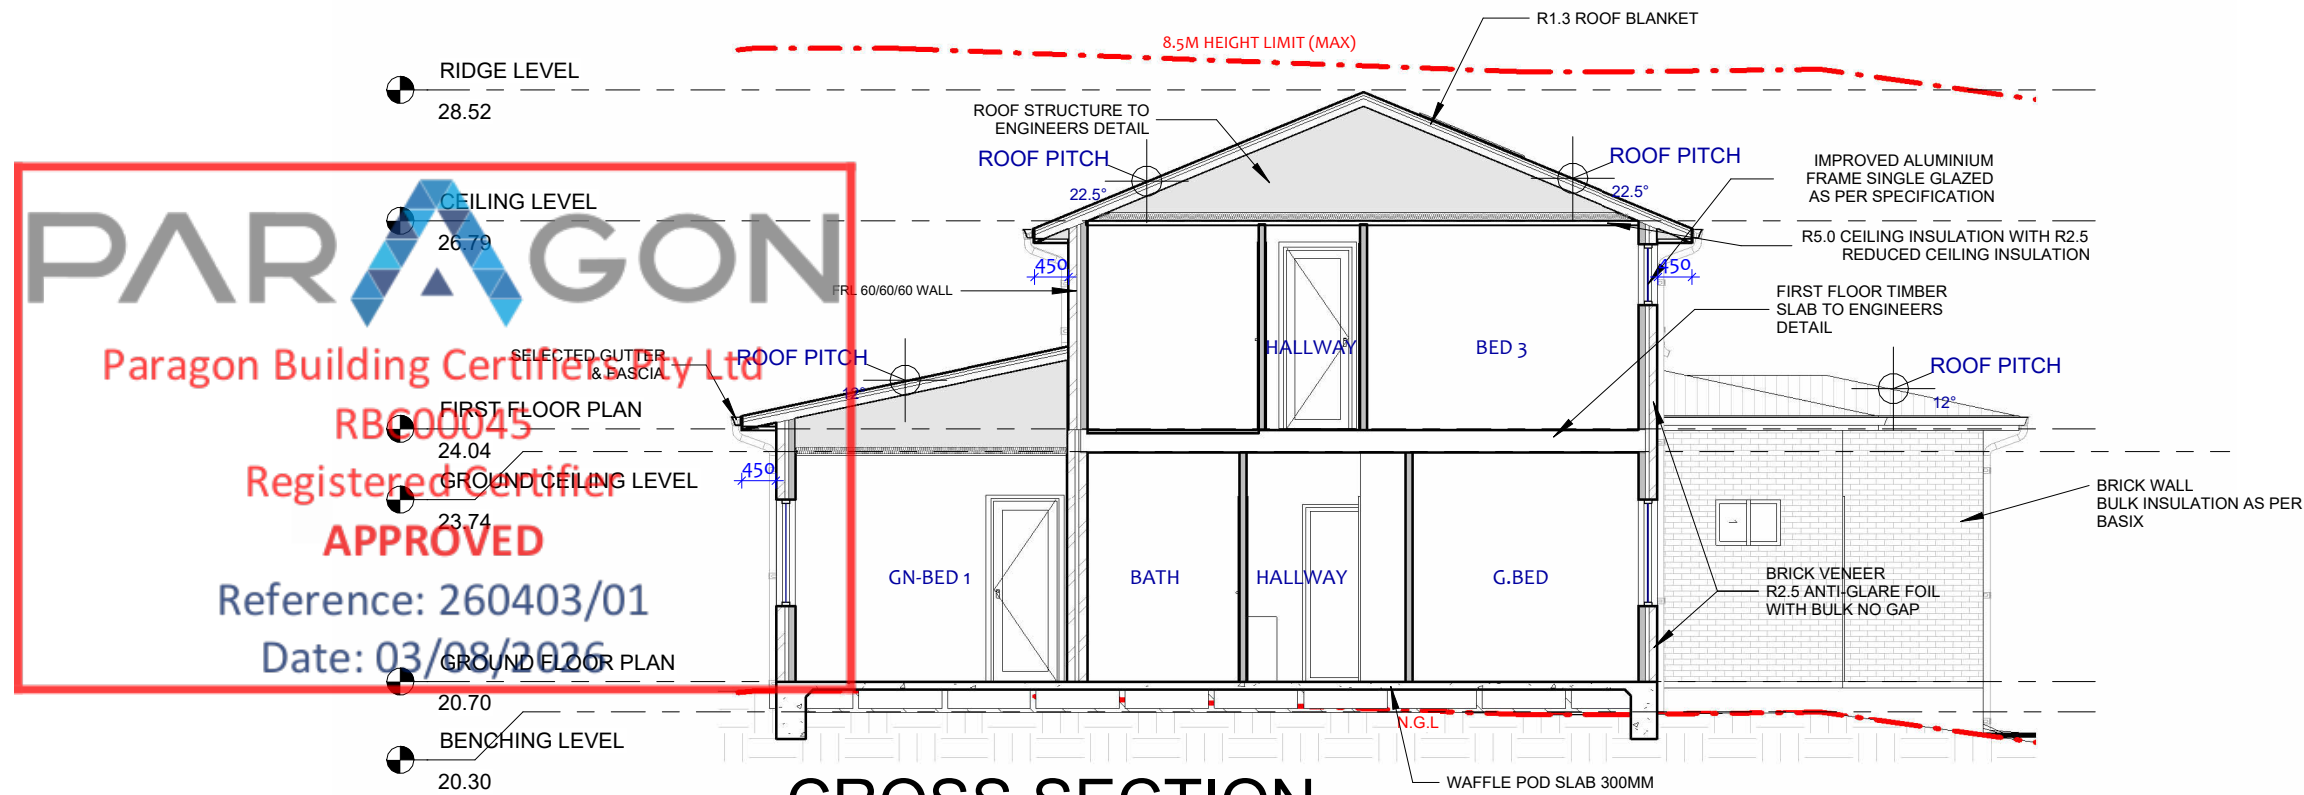

1 CROSS SECTION
1 : 100

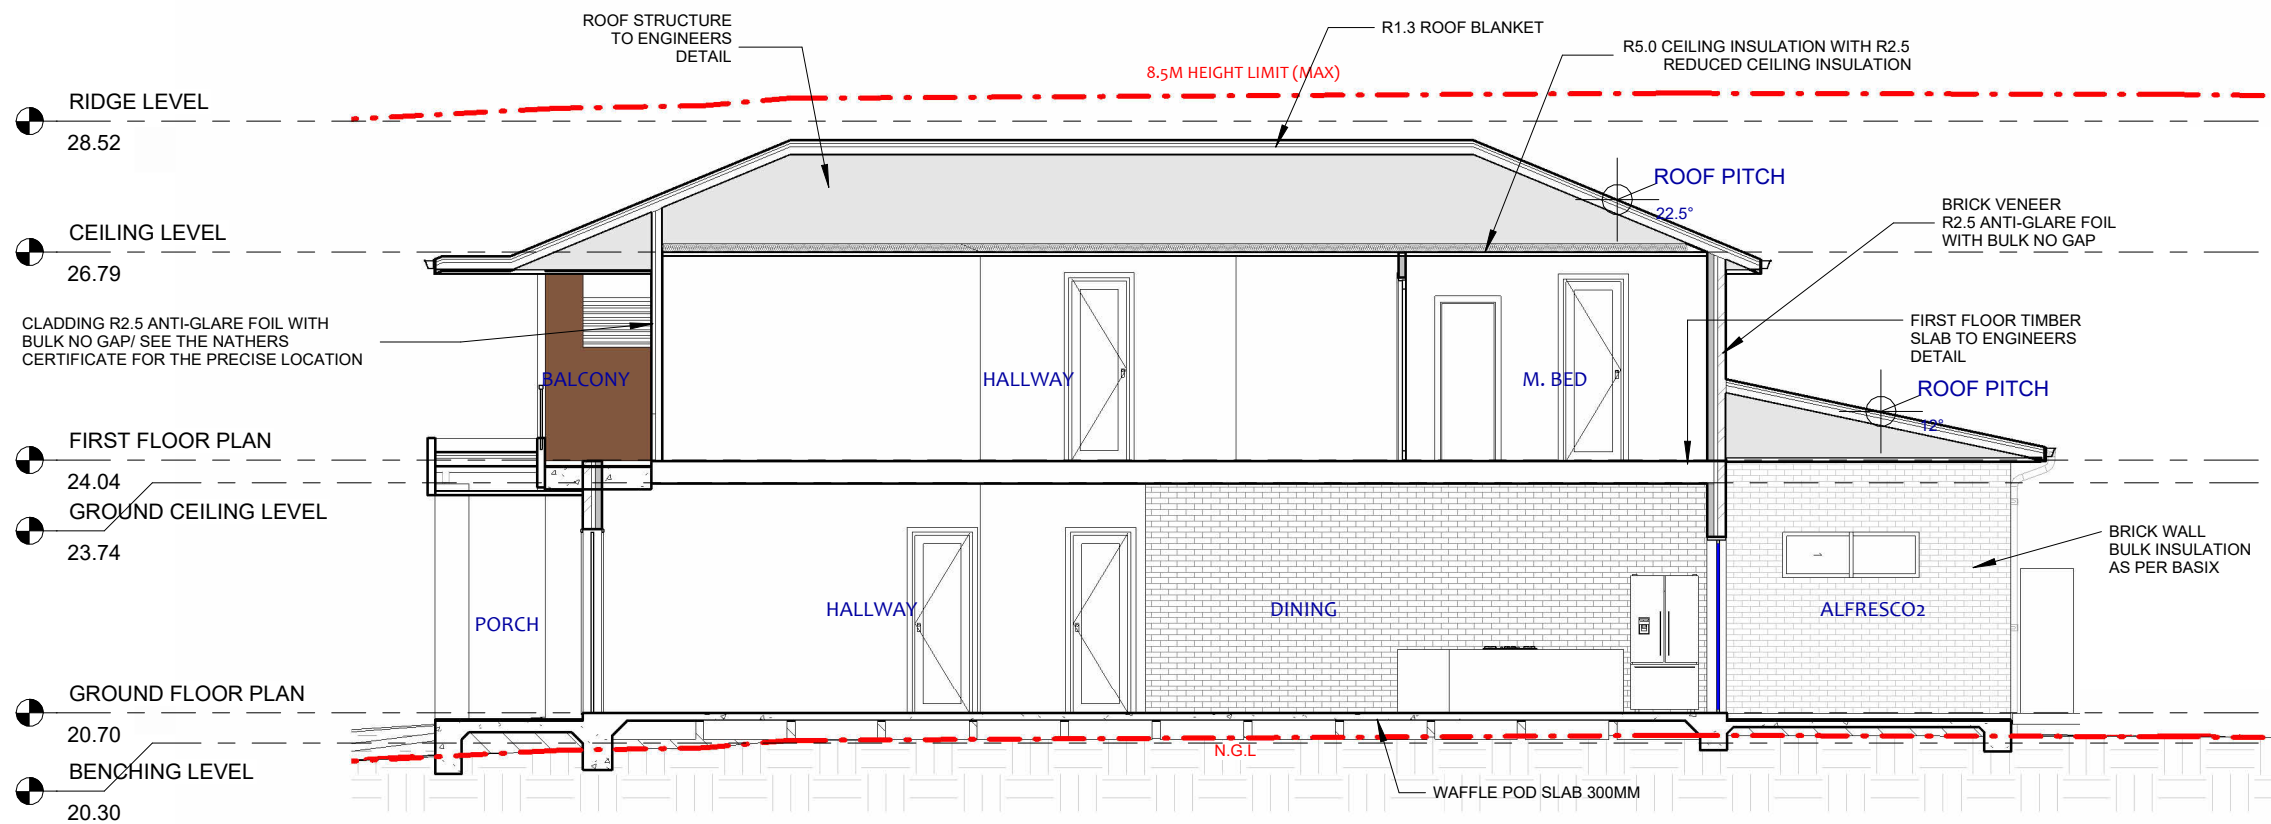

2 LONGITUDINAL SECTION
1 : 100


REV	DATE	DESCRIPTION	BY
11	17-04-2026	DA ISSUE	




RUBY
HOMES

THIS DRAWING IS THE EXCLUSIVE PROPERTY OF THE DEVELOPER & THE REPRODUCTION OF ANY PART WITHOUT THE PRIOR WRITTEN CONSENT OF THE DEVELOPER IS A VIOLATION OF APPLICABLE LAWS. IN NO EVENT SHALL THE DEVELOPER BE HELD LIABLE FOR SPECIAL COLLATERAL, INCIDENTAL OR CONSEQUENTIAL LIABILITY IN CONNECTION WITH THE USE OF THIS DIGITAL DATA ONCE RELEASED FROM THE DEVELOPER'S OFFICE. THIS DRAWING IS TO BE READ & UNDERSTOOD IN CONJUNCTION WITH THE STRUCTURAL, MECHANICAL, ELECTRICAL & / OR ANY OTHER CONSULTANT'S DOCUMENTATION AS MAY BE APPLICABLE TO THE PROJECT PRIOR TO THE START OF ANY WORKS AND FOR ITS DURATION.


PROJECT: Residential Building LOT 10 IN DP 263073 No.17 ADAM PLACE MACQUARIE FIELDS NSW 2564	DRAWING TITLE: SECTIONS	NORTH:	LOT NO: 10	DATE: 21-07-2026	SCALE: 1 : 100	DRAWING No: CC.10	REV: 11
			DRAWN BY: ROHIT	CHECKED BY: RH		ISSUED BY:	
			DRAFTED BY: ROHIT	CLIENT NAME: Anila Gurung & Amodh Gurung			

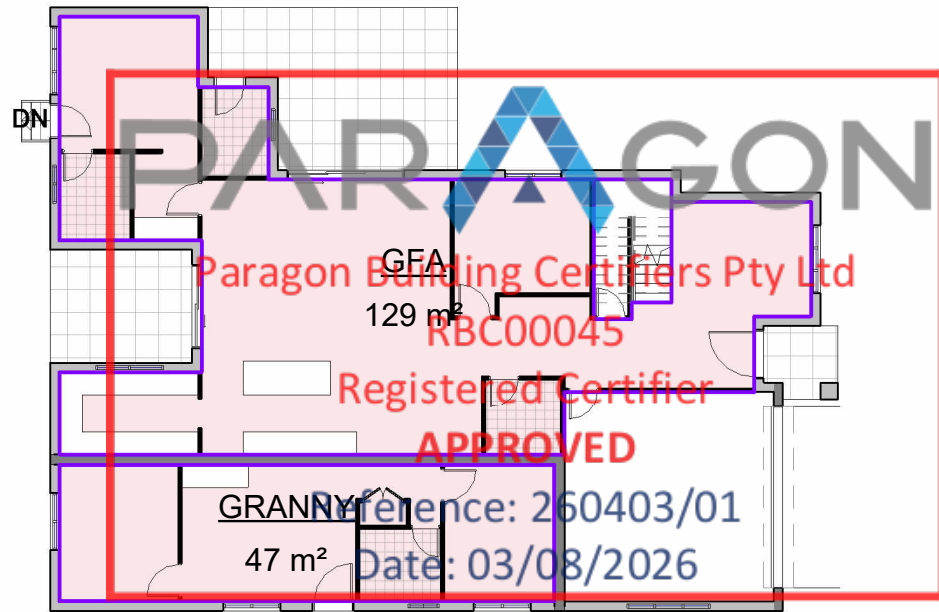


1 GROUND FLOOR PLAN
1 : 200

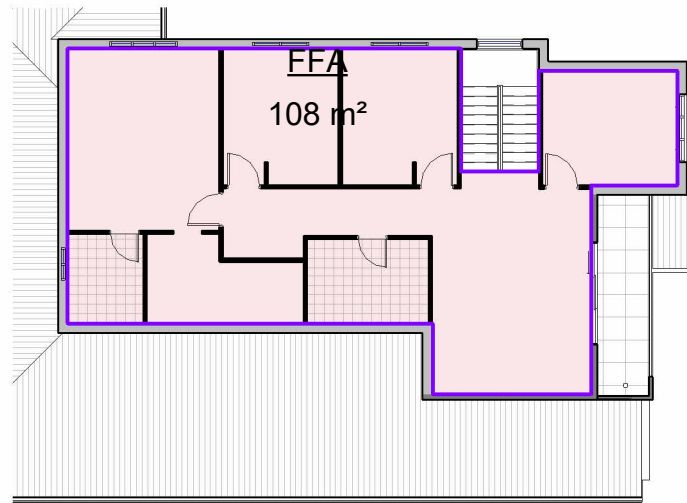

2 FIRST FLOOR PLAN
1 : 200

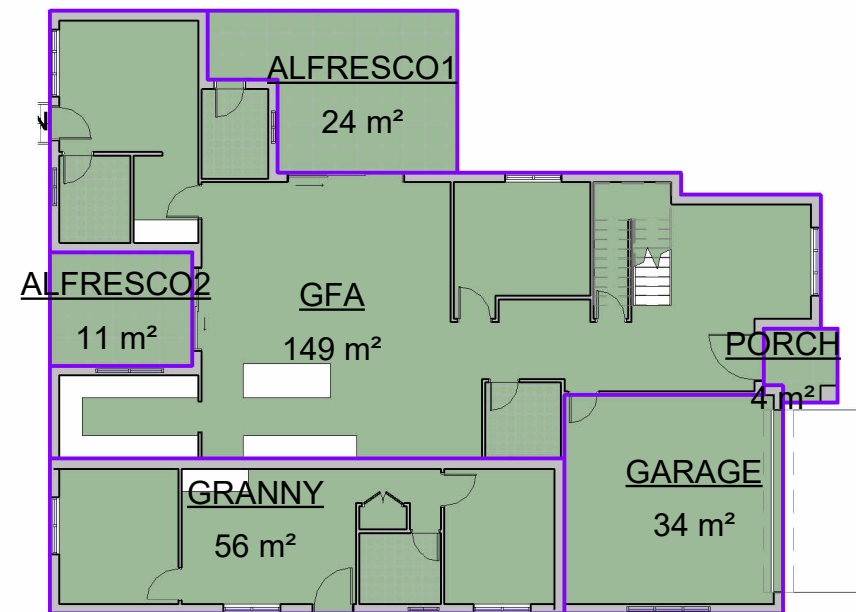

3 GROUND FLOOR PLAN
1 : 200

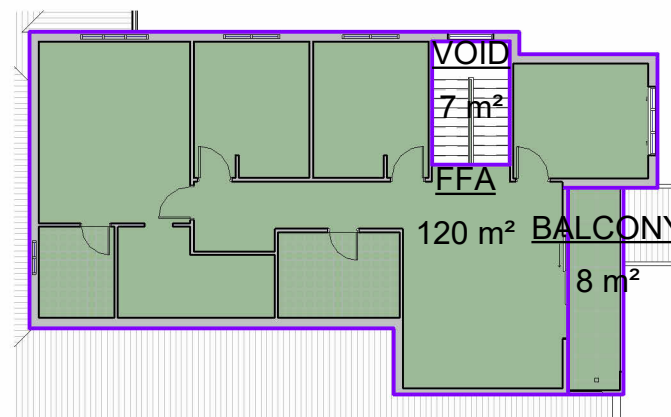

4 FIRST FLOOR PLAN
1 : 200

Area Schedule (FSR CALCULATION)	
Name	Area

GROUND FLOOR PLAN

GFA	129 m ²
GRANNY	47 m ²

GROUND FLOOR PLAN: 2 176 m²

FIRST FLOOR PLAN

FFA	108 m ²
-----	--------------------

FIRST FLOOR PLAN: 1 108 m²

Grand total: 3 284 m²

Area Schedule (Gross Building)	
Name	Area

GROUND FLOOR PLAN

GFA	149 m ²
GARAGE	34 m ²
PORCH	4 m ²
GRANNY	56 m ²
ALFRESCO1	24 m ²
ALFRESCO2	11 m ²

GROUND FLOOR PLAN: 6 277 m²


FIRST FLOOR PLAN

FFA	120 m ²
VOID	7 m ²
BALCONY	8 m ²

FIRST FLOOR PLAN: 3 135 m²


Grand total: 9 412 m²

				CC ISSUE											
				 THIS DRAWING IS THE EXCLUSIVE PROPERTY OF THE DEVELOPER & THE REPRODUCTION OF ANY PART WITHOUT THE PRIOR WRITTEN CONSENT OF THE DEVELOPER IS A VIOLATION OF APPLICABLE LAWS. IN NO EVENT SHALL THE DEVELOPER BE HELD LIABLE FOR SPECIAL COLLATERAL, INCIDENTAL OR CONSEQUENTIAL LIABILITY IN CONNECTION WITH THE USE OF THIS DIGITAL DATA ONCE RELEASED FROM THE DEVELOPER'S OFFICE. THIS DRAWING IS TO BE READ & UNDERSTOOD IN CONJUNCTION WITH THE STRUCTURAL, MECHANICAL, ELECTRICAL & / OR ANY OTHER CONSULTANT'S DOCUMENTATION AS MAY BE APPLICABLE TO THE PROJECT PRIOR TO THE START OF ANY WORKS AND FOR ITS DURATION.	PROJECT: Residential Building LOT 10 IN DP 263073 No.17 ADAM PLACE MACQUARIE FIELDS NSW 2564	DRAWING TITLE: AREA CALCULATION PLAN		LOT NO:	DATE:	SCALE: 1 : 200	DRAWING No: CC.11	REV:			
									11						
									ISSUED BY:						
11	17-04-2026	DA ISSUE													
REV	DATE		DESCRIPTION	BY				DRAWN BY: ROHIT	CHECKED BY: RH						
								DRAFTED BY: ROHIT	CLIENT NAME: Anila Gurung & Amodh Gurung						

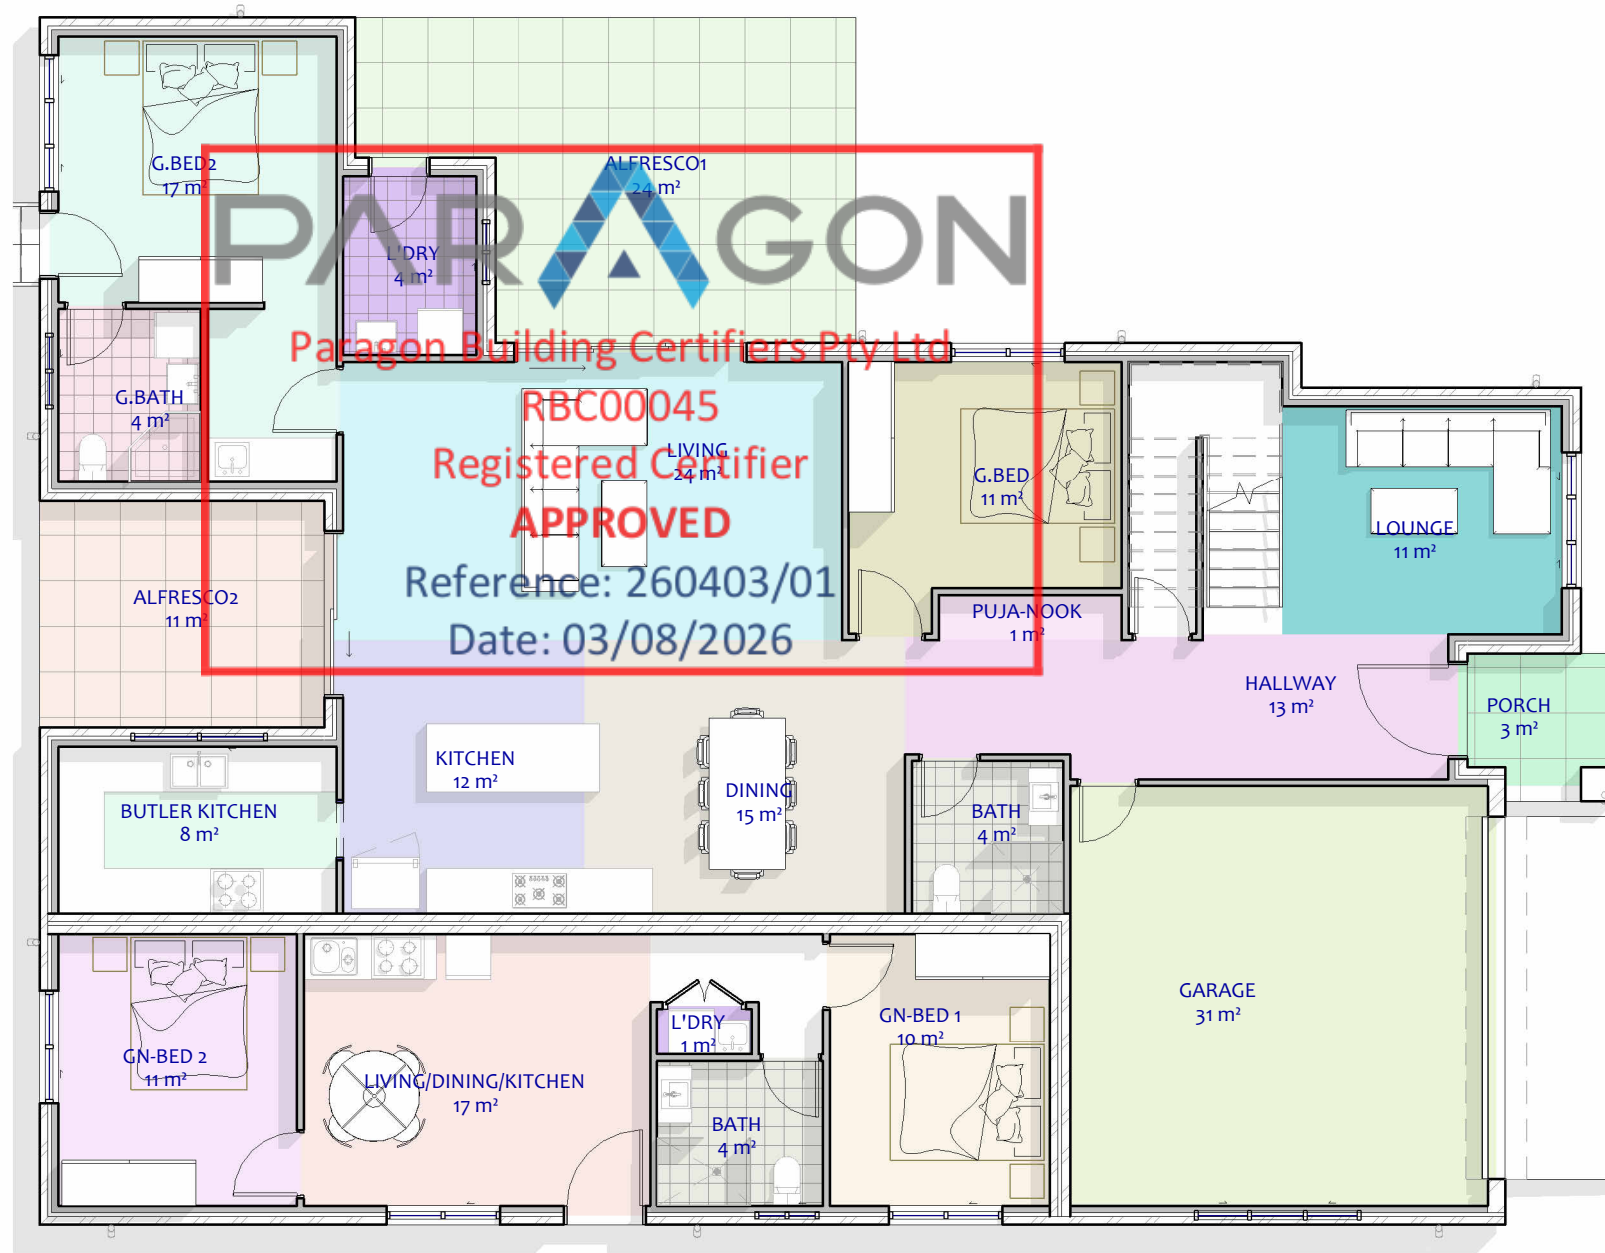

1 GROUND FLOOR ROOM AREA PLAN
 1 : 100

- | | | |
|----------------|----------|-----------------------|
| ALFRESCO1 | G.BED2 | LIVING |
| ALFRESCO2 | GARAGE | LIVING/DINING/KITCHEN |
| BATH | GN-BED 1 | LOUNGE |
| BUTLER KITCHEN | GN-BED 2 | PORCH |
| DINING | HALLWAY | PUJA-NOOK |
| G.BATH | KITCHEN | |
| G.BED | L'DRY | |

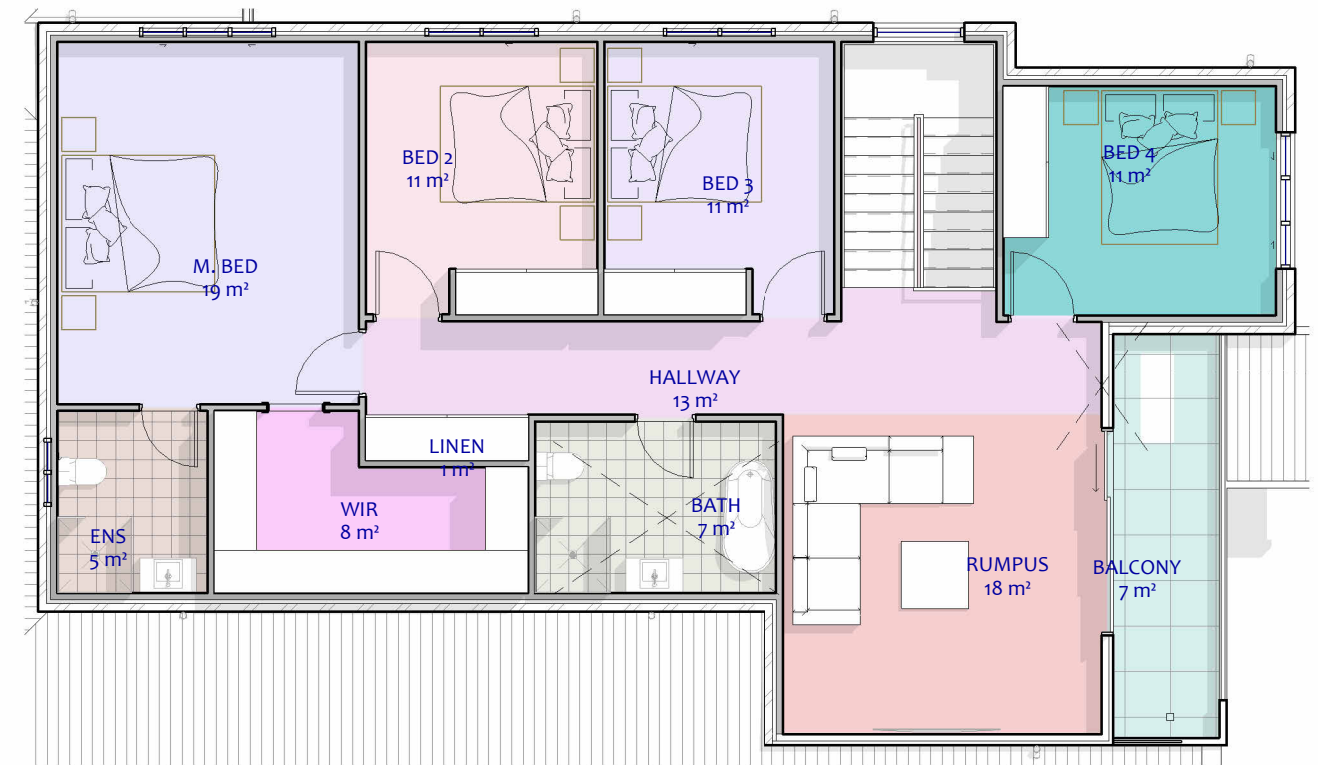

2 FIRST FLOOR ROOM AREA PLAN
 1 : 100

- | | |
|---------|----------------|
| BALCONY | LINEN |
| BATH | LOUNGE |
| BED 2 | M. BED |
| BED 3 | RUMPUS |
| BED 4 | STAIRCASE VOID |
| ENS | WIR |
| G.BED2 | |
| HALLWAY | |
| L'DRY | |


11	17-04-2026	DA ISSUE	
REV	DATE	DESCRIPTION	BY

RUBY HOMES

THIS DRAWING IS THE EXCLUSIVE PROPERTY OF THE DEVELOPER & THE REPRODUCTION OF ANY PART WITHOUT THE PRIOR WRITTEN CONSENT OF THE DEVELOPER IS A VIOLATION OF APPLICABLE LAWS. IN NO EVENT SHALL THE DEVELOPER BE HELD LIABLE FOR SPECIAL COLLATERAL, INCIDENTAL OR CONSEQUENTIAL LIABILITY IN CONNECTION WITH THE USE OF THIS DIGITAL DATA ONCE RELEASED FROM THE DEVELOPER'S OFFICE. THIS DRAWING IS TO BE READ & UNDERSTOOD IN CONJUNCTION WITH THE STRUCTURAL, MECHANICAL, ELECTRICAL & / OR ANY OTHER CONSULTANT'S DOCUMENTATION AS MAY BE APPLICABLE TO THE PROJECT PRIOR TO THE START OF ANY WORKS AND FOR ITS DURATION.

PROJECT:
 Residential Building
 LOT 10 IN DP 263073
 No.17 ADAM PLACE MACQUARIE
 FIELDS NSW 2564

DRAWING TITLE:
ROOM AREA PLAN

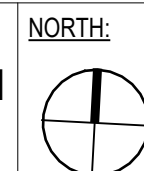

LOT NO: 10	DATE: 21-07-2026	SCALE: 1 : 100	DRAWING No:	REV: 11
DRAWN BY: ROHIT	CHECKED BY: RH		CC.12	ISSUED BY:
DRAFTED BY: ROHIT	CLIENT NAME: Anila Gurung & Amodh Gurung			



Paragon Building Certifiers Pty Ltd

RBC00045

Registered Certifier

APPROVED

Reference: 260403/01

Date: 03/08/2026



	1. RF	2. BR1	3. CD1	4. CR1	5. AL	6. ED	7. GD	8. FAS	9. GUT
	ROOF	MAIN WALLS	CLADDING	ACCENT 1/RENDER	WINDOWS/ BALUSTRADE	MAIN DOOR	GARAGE DOOR	FINISH	GUTTER
MATERIAL	COLORBOND DARK MONUMENT	HEBEL	BLUEBOARD	BRICK	ALUMINIUM	TIMBER	COLORBOND	TEXTURE PAINT	COLORBOND
COLOUR									

NOTE: ALL COLOURS SPECIFIED ARE INDICATIVE ONLY AND ARE SUBJECT TO VARIATION AND TO AVAILABILITY
ANY DISCREPANCY PLEASE FOLLOW AS PER RENDERED IMAGE

REV	DATE	DESCRIPTION	BY
11	17-04-2026	DA ISSUE	



THIS DRAWING IS THE EXCLUSIVE PROPERTY OF THE DEVELOPER & THE REPRODUCTION OF ANY PART WITHOUT THE PRIOR WRITTEN CONSENT OF THE DEVELOPER IS A VIOLATION OF APPLICABLE LAWS. IN NO EVENT SHALL THE DEVELOPER BE HELD LIABLE FOR SPECIAL COLLATERAL, INCIDENTAL OR CONSEQUENTIAL LIABILITY IN CONNECTION WITH THE USE OF THIS DIGITAL DATA ONCE RELEASED FROM THE DEVELOPER'S OFFICE. THIS DRAWING IS TO BE READ & UNDERSTOOD IN CONJUNCTION WITH THE STRUCTURAL, MECHANICAL, ELECTRICAL & / OR ANY OTHER CONSULTANT'S DOCUMENTATION AS MAY BE APPLICABLE TO THE PROJECT PRIOR TO THE START OF ANY WORKS AND FOR ITS DURATION.

PROJECT:
Residential Building
LOT 10 IN DP 263073
No.17 ADAM PLACE MACQUARIE
FIELDS NSW 2564

DRAWING TITLE:
COLOR SCHEDULE

NORTH:

LOT NO:
10
DRAWN BY:
ROHIT
DRAFTED BY:
ROHIT

DATE:
21-07-2026
CHECKED BY:
RH
CLIENT NAME:
Anila Gurung & Amodh Gurung

SCALE:
1 : 100



DRAWING No:
CC.13

REV:
11
ISSUED BY:

CC ISSUE

COMPLIANCE NOTES:

Switchboards, air conditioning units, garabage storage areas and storage for other utilities must not be attached to the front elevations of the building or side elevations that can be seen from a public place.

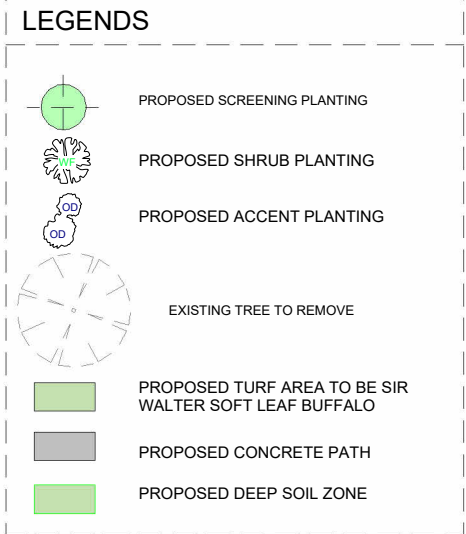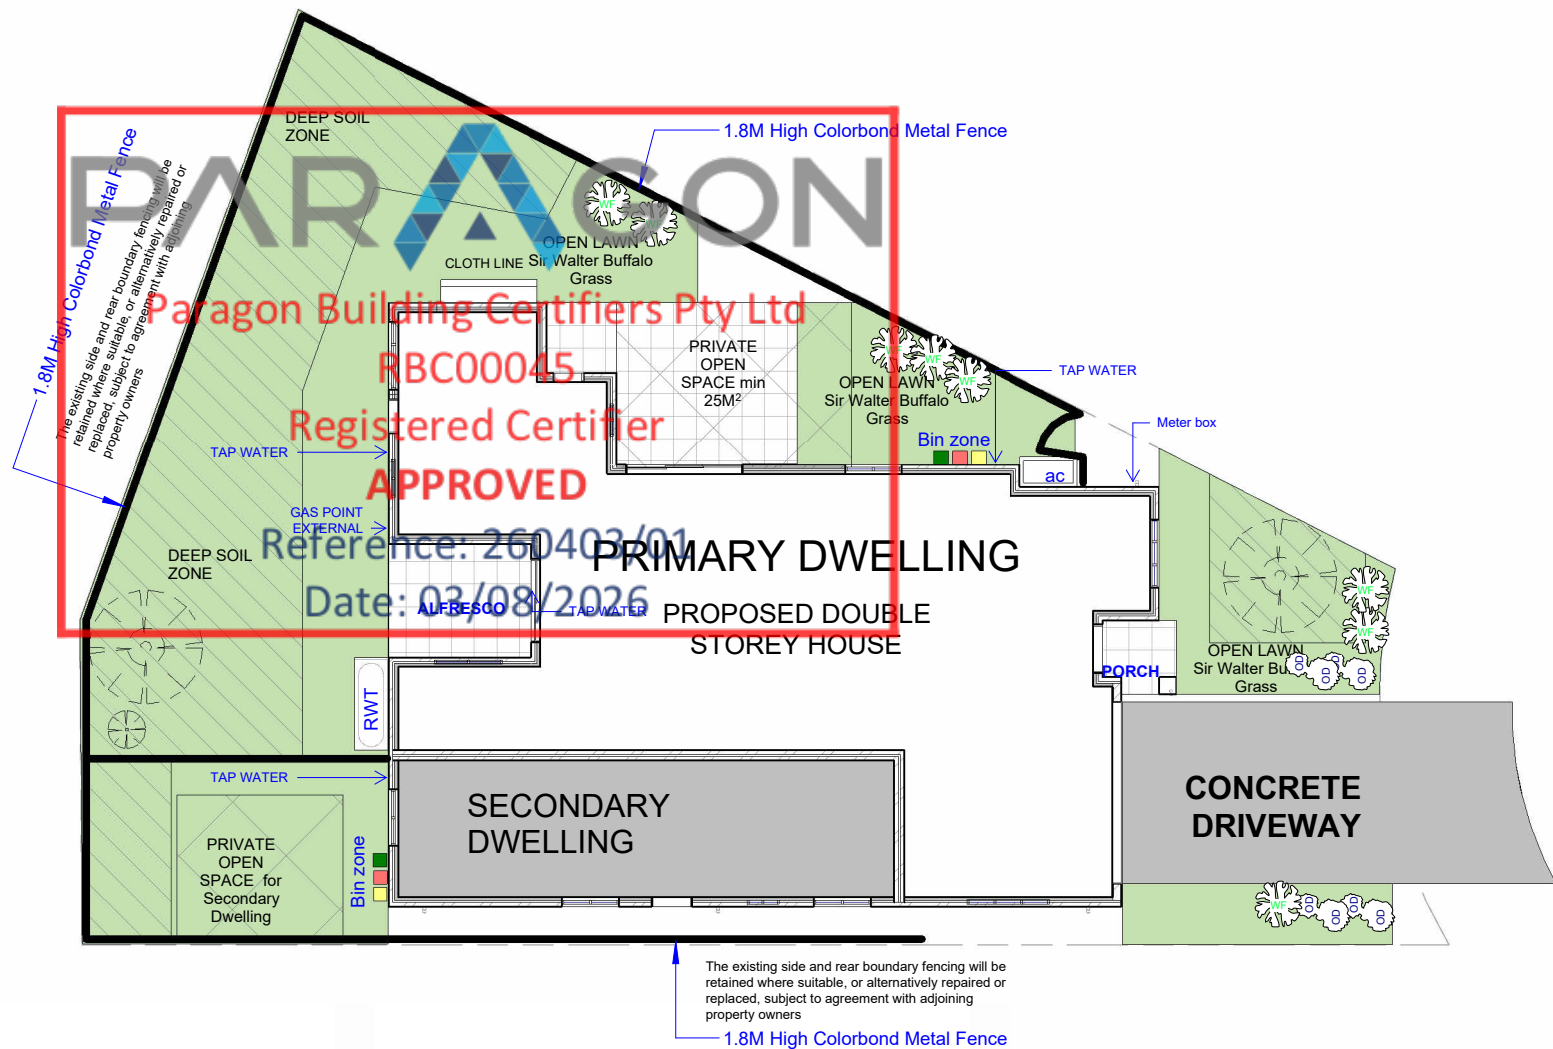

1 CDC - SITE LANDSCAPE
1 : 200

GENERAL NOTES:

- LANDSCAPE CONTRACTOR TO CHECK DA CONDITIONS AND STAMPED LANDSCAPE PLAN BEFORE COMMENCING WORKS TO ENSURE NO ADDITIONS/AMENDMENTS TO PLAN.
- GARDEN BEDS IN OSD BASIN TO CONSIST OF NON FLOATABLE DECORATIVE GRAVEL.
- REFER TO HYDRAULICS ENGINEERS PLAN FOR OSD DETAILS/FINAL LEVELS.
- MULCHED PLANTING BEDS TO BE A MINIMUM DEPTH OF 75mm AS SELECTED.
- CONTRACTOR'S RESPONSIBILITY TO CHECK AND ADJUST SOIL pH AS REQUIRED.
- PROVIDE TIMBER EDGE AS A MINIMUM BENEATH FENCING/GATES TO DEFINE TURF AND GARDEN BEDS/PATHWAYS.EDGING TO BE PROVIDED TO ALL AREAS WHERE DIFFERING MATERIALS MEET i.e TURF/GARDEN,TURF/GRAVEL PATH ETC.
- WEED MAT BENEATH GRAVEL GRAVEL PATHWAYS REQUIRED TO LIMIT MUD TRACKING.
- PREMIUM ORGANIC GARDEN MIX TO BE USED.
- ALL PLANTS TO BE HEALTHY AND VIGOROUS.
- CONTRACTOR TO MAKE GOOD TURF ON NATURE STRIP POST CONSTRUCTION
- CONTRACTOR TO MAKE GOOD TURF ON NATURE STRIP POST CONSTRUCTION.
- DO NOT SCALE ARCHITECTURAL SETOUT FROM LANDSCAPE DRAWING.
- EXISTING TREE SPREAD APPROXIMATE ONLY.REFER TO TREE REPORT WHEN APPLICABLE.
- SITE SURVEY PROVIDED BY OTHERS.
- BUFFALO TURF PREFERRED OVER KIKUYU.

LANDSCAPE BASIX NOTE:
THE APPLICANT MUST PLANT INDIGENEOUS OR LOW WATER USE SPECIES OF VEGETATION THROUGHOUT 15 SQM OF THE SITE.

NOTE :BUILDER RESERVES THE RIGHT NOT TO UNDERTAKE NOR SUPPLY CERTIFICATE FOR OCCUPATION CERTIFICATE.
NOTE : TO AID COMPLIANCE WITH BASIX LEGISLATION,PLANTS (WHERE APPLICABLE) HAVE BEEN SELECTED FROM THE LOCAL CITY COUNCIL/SHIRE PLANT LISTS.
NOTE: LOCATION OF SEWER MAINS/LINES,WATER PIPES,UNDERGROUND ELECTRICITY AND OTHER SERVICES MUST BE OBTAINED PRIOR TO COMMENCEMENT OF ANY WORK ON SITE.

CONTRACTORS NOTE : CALCULATED ARES DETERMINED BY CAD AND HAVE BEEN ROUNDED UP FOR USE AS A GUIDE ONLY ALLOW STANDARD PERCENTAGE FOR CUTTING AND WASTAGE .CONFIRM DIMENSIONS AND NUMBERS PRIOR TO QUOTING/ORDERING.

LANDSCAPE AREA


TOTAL LANDSCAPE AREA	245.0m ²
FRONT AREA	60.0m ²
REAR AREA	185.0 m ²
Deep Soil Planting: (min 20% of Lot 598.4m ²)	119.6m ²

PLANT SCHEDULE

Genus	Common Name	Qty	Pot size	Height	width
Trees					
Banksia integrifolia	coast banksia	1	45L	7	4
Cupaniopsis anacardioides	Tuckeroo	1	45L	8	4
Shrubs					
Grevillea 'moonlight'	Grevillea Moonlight	-	140mm	3	1.5
Leptospermum 'Cardwell'	Tea Tree	-	140mm	1.5	1
Leucophyta Brownii	Cushion Bush	-	140mm	1.5	1
Westringia Fruticosa	Coastal Rosemary	-	140mm	1.5	2
Accents					
Agave Americana	American Aloe	-	200mm	1.5	1.5

CC ISSUE

REV	DATE	DESCRIPTION	BY
11	17-04-2026	DA ISSUE	

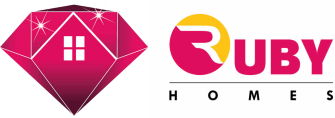
THIS DRAWING IS THE EXCLUSIVE PROPERTY OF THE DEVELOPER & THE REPRODUCTION OF ANY PART WITHOUT THE PRIOR WRITTEN CONSENT OF THE DEVELOPER IS A VIOLATION OF APPLICABLE LAWS. IN NO EVENT SHALL THE DEVELOPER BE HELD LIABLE FOR SPECIAL COLLATERAL, INCIDENTAL OR CONSEQUENTIAL LIABILITY IN CONNECTION WITH THE USE OF THIS DIGITAL DATA ONCE RELEASED FROM THE DEVELOPER'S OFFICE. THIS DRAWING IS TO BE READ & UNDERSTOOD IN CONJUNCTION WITH THE STRUCTURAL, MECHANICAL, ELECTRICAL & / OR ANY OTHER CONSULTANT'S DOCUMENTATION AS MAY BE APPLICABLE TO THE PROJECT PRIOR TO THE START OF ANY WORKS AND FOR ITS DURATION.

PROJECT:
Residential Building
LOT 10 IN DP 263073
No.17 ADAM PLACE MACQUARIE
FIELDS NSW 2564

DRAWING TITLE:
LANDSCAPE PLAN



LOT NO: 10	DATE: 21-07-2026	SCALE: 1 : 200	DRAWING No:	REV: 11
DRAWN BY: ROHIT	CHECKED BY: RH		CC.14	ISSUED BY:
DRAFTED BY: ROHIT	CLIENT NAME: Anila Gurung & Amodh Gurung			



/for details: See the Basix certificate/

The applicant must install a Central rainwater tank of at least 2000 litres.
The rainwater tank to collect rain runoff from at least 270 m2 of the roof /See the central systems/
The applicant must connect the rainwater tank to:

- all toilets
- all laundries
- the rainwater tank to allow irrigation of min. 246 m2, common landscaping in the development /See the central systems/

- Shower heads 3 star (> 7.5 but <= 9.0 L/min)
- Toilets.....4 star
- Kitchen tap.....5 star
- Basin Taps.....5 star


Heating/Cooling: 3-phase air-conditioning; Energy rating: EER 2.5-3.0 (Zoned) (Main Dwelling)
Heating/Cooling: 1-phase air-conditioning; Energy rating: 3* average zone (Living ONLY) (Secondary Dwelling)

Natural lighting: Window/skylight in 2 Bathrooms/Toilets(Main Dwelling)
Natural lighting: Window/skylight in 1 Bathrooms/Toilets(Sec. Dwelling)

- The applicant must ensure that a minimum of 80% of light fixtures are fitted with fluorescent, compact fluorescent, or light-emitting-diode (LED) lamps.

- The applicant must install a gas cooktop & electric oven in the kitchen of each dwelling.
- The applicant must install a fixed outdoor clothes drying line for each dwelling.

- The applicant must install a photovoltaic system as part of the development. The applicant must connect this system to the development's electrical system.
- The photovoltaic system must consist of photovoltaic collectors with the capacity to generate at least 1 peak kilowatts of electricity, installed at an angle between 10 degrees and 25 degrees to the horizontal facing north.

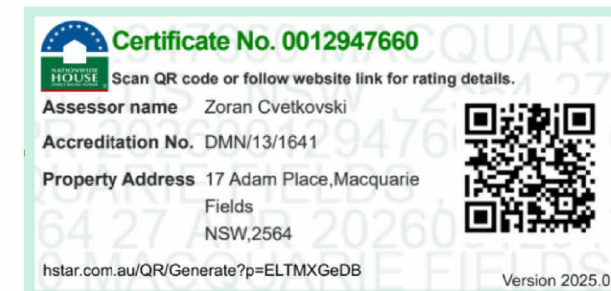

/For Details: see the Nathers certificate

A detailed method of assessment with greater flexibility of solution choice and capacity to assess complex dwelling designs.

- Timber Stud Frame Brick Veneer, R2.5 Anti-glare foil with bulk no gap
- Fibro Timber Stud Frame Panel on Battens, R2.5 Anti-glare foil with bulk no gap

- Timber Stud Frame, Direct Fix Plasterboard, R2.5 Bulk Insulation, No Air Gap (Against Garage)
- Timber Stud Frame, Direct Fix Plasterboard No Insulation (All Others)
- Cavity brick, plasterboard, No Insulation (Neighbouring Wall)

- Waffle pod slab

- Timber Framed Timber Above Plasterboard, R2.5 Bulk Insulation (Above Garage)
- Timber Framed Timber Above Plasterboard, No Insulation (All Others)

- Plasterboard on Timber, R2.5 Bulk Insulation Unventilated roofspace (Reduced insulation near the eave in the distance of 580mm)
- Plasterboard on Timber, R5.0 Bulk Insulation Unventilated roofspace (All others/unaffected ceiling area)

- Corrugated Iron Timber Frame, R1.3 Bulk, Reflective Side Down, No Air Gap Above

Note: All downlights: IC-F /IC-4/ (insulation covered/ including the control gears/) rated as per AS/NZS standard 60598 and IP (sealed) rated as per BS EN 60529:1992, European IEC 60509:1989

Note: (where the roof is extended over an open area such as a deck or carport): A barrier to be installed within the roof space to separate the space above the zoned part of the house and the space above the open veranda.
 Note-Ceiling fans: For the number and the location, see the Nathers certificate.

For additional information please refer to the additional notes on the Nathers certificate.

Unit	Description
Mn Dw	Main Dwelling
Sc Dw	Secondary Dwelling

				CC ISSUE							
				 PROJECT: Residential Building LOT 10 IN DP 263073 No.17 ADAM PLACE MACQUARIE FIELDS NSW 2564	<u>DRAWING TITLE:</u> BASIX COMMITMENTS	<u>NORTH:</u>	LOT NO: 10	DATE: 21-07-2026	SCALE:	<u>DRAWING No:</u> CC.15	<u>REV:</u> 11
							DRAWN BY: RUBY	CHECKED BY: RH		ISSUED BY:	
11	17-04-2026	DA ISSUE					DRAFTED BY: ROHIT	CLIENT NAME: Anila Gurung & Amodh Gurung			
REV	DATE	DESCRIPTION	BY								

Window Schedule 1				
Mark	Height	Width	Head Height	Description

GROUND FLOOR PLAN

GW1	1850	1800	2400	SLIDING AND FIXED
GW2	1400	1500	2400	SLIDING
GW3	600	850	2400	SLIDING
GW4	600	1800	2400	SLIDING
GW5	600	2100	2400	SLIDING AND FIXED
GW6	1850	1800	2400	SLIDING AND FIXED
GW7	800	1000	2400	SLIDING

GROUND FLOOR PLAN: 7

FIRST FLOOR PLAN

FW1	1850	1800	2450	SLIDING AND FIXED
FW2	2050	1200	2450	FIXED
FW3	800	1500	2450	SLIDING
FW4	800	1500	2450	SLIDING
FW5	1250	1800	2450	SLIDING AND FIXED
FW6	800	900	2450	SLIDING

FIRST FLOOR PLAN: 6

Window Schedule 2				
Mark	Height	Width	Head Height	Description

GROUND FLOOR PLAN

GN-GW1	1400	1500	2400	SLIDING
GN-GW2	1400	1500	2400	SLIDING
GN-GW3	600	850	2400	SLIDING
GN-GW4	1400	1500	2400	SLIDING

GROUND FLOOR PLAN: 4

Door Schedule 1			
Mark	Height	Width	Description

GROUND FLOOR PLAN

D1	2340	720	FLUSH DOOR
D2	2340	720	FLUSH DOOR
D3	2340	720	FLUSH DOOR
D4	2340	820	FLUSH DOOR
D5	2340	820	FLUSH DOOR
D6	2340	720	FLUSH DOOR
D7	2340	1100	FLUSH DOOR
D8	2340	1000	FLUSH DOOR
D9	2340	820	FLUSH DOOR
D10	2340	820	FLUSH DOOR
D11	2340	720	FLUSH DOOR
D12	2340	820	FLUSH DOOR
D13	2340	720	FLUSH DOOR
GD	2400	4800	GARAGE DOOR
MD	2400	1200	SOLID CORE DOOR
SD1	2300	3000	SLIDING DOOR
SD2	2300	2200	SLIDING DOOR

GROUND FLOOR PLAN: 17

FIRST FLOOR PLAN

D14	2340	820	FLUSH DOOR
D15	2340	820	FLUSH DOOR
D16	2340	720	FLUSH DOOR
D17	2340	820	FLUSH DOOR
D18	2340	820	FLUSH DOOR
D19	2340	720	FLUSH DOOR
SD3	2300	2650	SLIDING DOOR

FIRST FLOOR PLAN: 7


11	17-04-2026	DA ISSUE	
10	26-03-2026	Rendered Pillar and Porch cover with only flashing added - Ekta	
7	26-02-2026	Bank Set	
REV	DATE	DESCRIPTION	BY



THIS DRAWING IS THE EXCLUSIVE PROPERTY OF THE DEVELOPER & THE REPRODUCTION OF ANY PART WITHOUT THE PRIOR WRITTEN CONSENT OF THE DEVELOPER IS A VIOLATION OF APPLICABLE LAWS. IN NO EVENT SHALL THE DEVELOPER BE HELD LIABLE FOR SPECIAL COLLATERAL, INCIDENTAL OR CONSEQUENTIAL LIABILITY IN CONNECTION WITH THE USE OF THIS DIGITAL DATA ONCE RELEASED FROM THE DEVELOPER'S OFFICE. THIS DRAWING IS TO BE READ & UNDERSTOOD IN CONJUNCTION WITH THE STRUCTURAL, MECHANICAL, ELECTRICAL & / OR ANY OTHER CONSULTANT'S DOCUMENTATION AS MAY BE APPLICABLE TO THE PROJECT PRIOR TO THE START OF ANY WORKS AND FOR ITS DURATION.

PROJECT:
Residential Building
LOT 10 IN DP 263073
No.17 ADAM PLACE MACQUARIE
FIELDS NSW 2564

DRAWING TITLE:
**DOOR WINDOW
SCHEDULE**

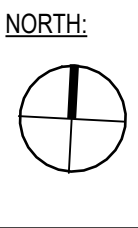

LOT NO:	10	DATE:	21-07-2026	SCALE:		DRAWING No:	CC.16	REV:	11
DRAWN BY:	AS	CHECKED BY:	RH					ISSUED BY:	
DRAFTED BY:	ROHIT	CLIENT NAME:	Anila Gurung & Amodh Gurung						

CC ISSUE

ABCB HOUSING PROVISIONS : PART 10.2 WET AREA WATERPROOFING

10.2.1 Wet Areas

1. Building elements in wet areas within a building must be protected with a waterproofing system.
2. The waterproofing system in (1) must be either waterproof or water resistant in accordance with 10.2.2 to 10.2.6.

10.2.2 Shower Areas (enclosed and unenclosed)

1. For a shower area with a hob, step-down or level threshold, the following applies:
- a. The floor of the shower area must be **waterproof**, including any hob or step-down (see Figure 10.2.2); and
- b. The walls of the shower area must be **waterproof** not less than 1800 mm above the floor substrate (see Figure 10.2.2).
- c. Wall junctions and joints within the shower area must be **waterproof** not less than 40 mm either side of the junction (see Figure 10.2.2).
- d. Wall/floor junctions within the shower area must be **waterproof** (see Figure 10.2.2).
- e. Penetrations within the shower area must be **waterproof**.
2. A shower with a **preformed shower base** must also comply with the requirements of (1), except for (a) which is not applicable.

Figure 10.2.2: Extent of treatment for shower areas - concrete compressed fibre-cement and fibre-cement sheet floors.

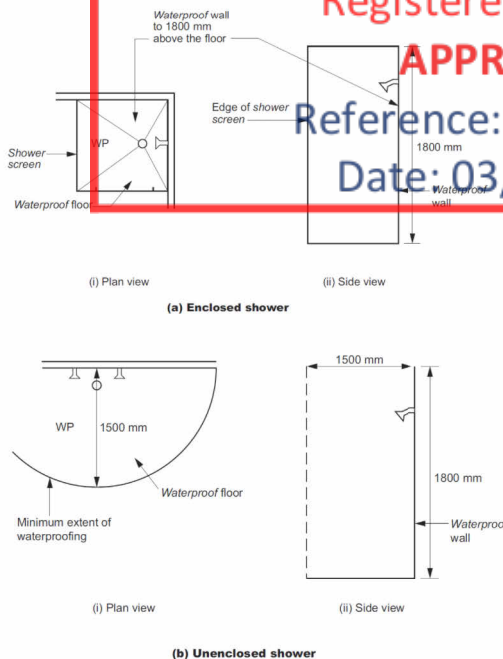


Figure Notes
Wall/floor junction heights are to be as per 10.2.2 to 10.2.6 (as applicable).

Notes
Where a shower is above a bath or spa, use requirements for shower.

10.2.3 Area outside shower area

1. For concrete, compressed fibre-cement and fibre-cement sheet flooring, the floor of the room must be water resistant.
2. For timber floors including particleboard, plywood and other timber based flooring materials, the floor of the room must be waterproof.
3. Wall/floor junctions must be -
- a. waterproof, and
- b. where a flashing is used, the horizontal leg must be not less than 40 mm.

10.2.4 Areas adjacent to baths and spas without showers

1. For areas adjacent to all baths and spas, the following applies:
- a. For concrete, compressed fibre-cement and fibre-cement sheet flooring, the floor of the room must be water resistant.
- b. For timber floors including particleboard, plywood and other timber based flooring materials, the floor of the room must be waterproof.
- c. Tap and spout penetrations must be waterproof where they occur in horizontal surfaces.
2. For areas adjacent to non-freestanding baths and spas, the following applies:
- a. Walls must be water resistant (see Figure 10.2.4a and Figure 10.2.4b)-
- to a height of not less than 150mm above the vessel, for the extent of the vessel, where the vessel is within 75mm of a wall; and
 - for all exposed surfaces below vessel lip.
- b. Wall junctions and joints must be water resistant within 150mm above a vessel for the extent of the vessel.
- c. Wall/floor junctions must be waterproof for the extent of the vessel (see Figure 10.2.4a and Figure 10.2.4b).
3. For inserted baths and spas, the following applies.
- a. For floors and horizontal surfaces:
- Any shelf area adjoining the bath or spa must be waterproof and include a waterstop under the vessel lip.
 - There are no requirements for the floor under a bath or spa.
- b. For walls:
- Waterproof to not less than 150mm above the lip of a bath or spa.
 - There are no requirements for the floor under a bath or spa.
- c. For wall junctions and joints, the following applies:
- Waterproof junctions within 150mm of a bath or spa.
 - There are no requirements for junctions and joints in walls beneath the lip of a bath or spa.
- d. Tap and spout penetrations must be waterproof where they occur in horizontal surfaces.

Figure 10.2.4a: Areas adjacent to baths and spas without showers for concrete, compressed fibre-cement and fibre-cement sheet flooring



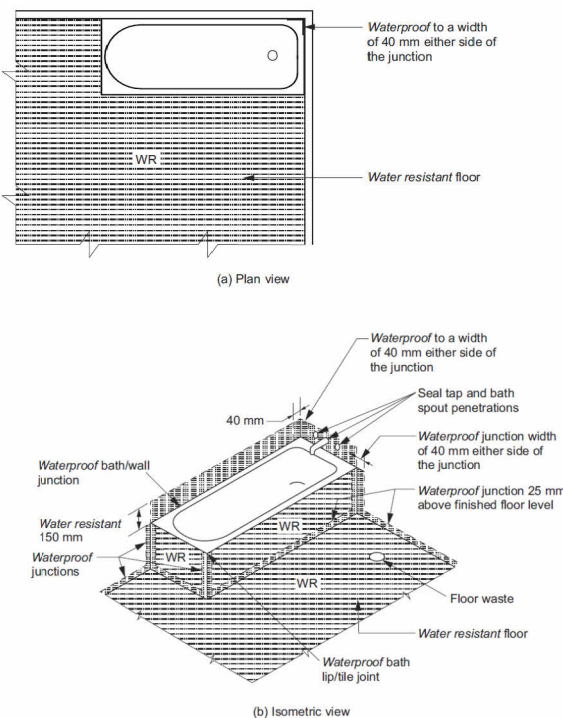



Figure 10.2.4b: Areas adjacent to baths and spas without showers for timber floors including particle-board, plywood and other floor materials

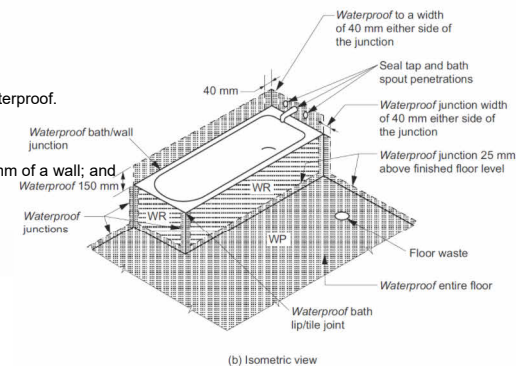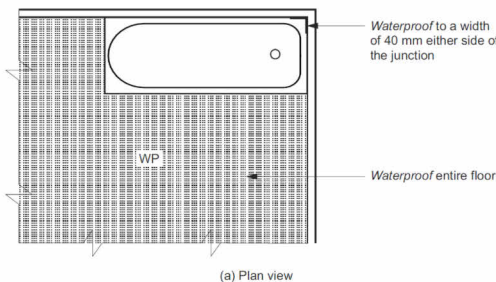

10.2.5 Other areas

1. For walls adjoining other types of vessels (e.g. sink, basin or laundry tub), the following applies:
- a. Walls must be water resistant to a height of not less than 150mm above the vessel, for the extent of the vessel, where the vessel is within 75 mm of a wall (see Figure 10.2.5.)
- b. Waterproof wall junctions where a vessel is fixed to a wall.
- c. Waterproof tap and spout penetrations where they occur in surfaces required to be waterproof or water resistant.
2. For laundries and WCs, the following applies:
- a. The floor of the room must be water resistant.
- b. Wall/floor junctions must be water resistant, and where a flashing is used, the horizontal leg must not be less than 40 mm.
3. For WCs with handheld bidet spray installations, the following applies:
- a. The floor of the room must be waterproof.
- b. Walls must be -
- waterproof in WC area within a 900 mm radius from the wall connection of the handheld bidet spray device to a height of not less than 150mm above the floor substrate; and
 - water resistant in WC area within a 900 mm radius from the wall connection of the handheld bidet device to not less than 1200 mm above the finished floor level of the WC.
- c. Wall junctions within the WC area within 900 mm radius from the wall connection of the handheld bidet spray device must be waterproof.
- d. Wall/floor junctions within the WC area within 1000 mm radius from the wall connection of the handheld bidet spray device must be waterproof.
- e. Penetrations in the WC area must be waterproof.

Figure 10.2.5: Bath and vessel abutting wall - areas to be protected

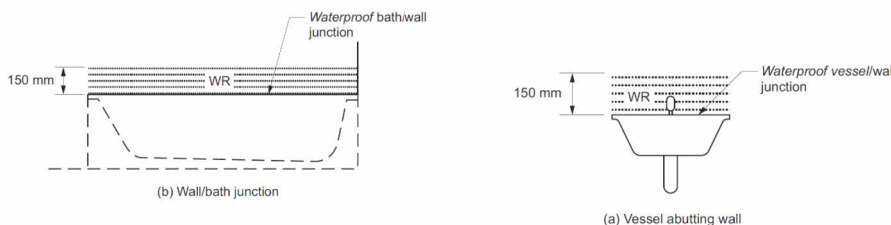

10.2.6 Waterproofing systems

1. For the purposes of this Part, a waterproofing system is deemed -
- a. waterproof, if it complies with (2); or
- b. water resistant, if it complies with (3).
2. For a waterproofing system required to be waterproof in accordance with 10.2.2 to 10.2.5, the materials nominated in 10.2.8 must be used.
3. For a waterproofing system required to be water resistant in accordance with 10.2.2 to 10.2.5, the materials nominated in 10.2.9 must be used in conjunction with the materials in 10.2.10.


10.2.12 Construction of wet area floors - falls

Where a floor waste is installed -

a. the minimum continuous fall of a floor plane to the waste must be 1:80; and

b. the maximum continuous fall of a floor plane to the waste must be 1:50.

REV	DATE	DESCRIPTION	BY
11	17-04-2026	DA ISSUE	
10	26-03-2026	Rendered Pillar and Porch cover with only flashing added - Ekta	
7	26-02-2026	Bank Set	

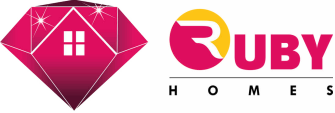

THIS DRAWING IS THE EXCLUSIVE PROPERTY OF THE DEVELOPER & THE REPRODUCTION OF ANY PART WITHOUT THE PRIOR WRITTEN CONSENT OF THE DEVELOPER IS A VIOLATION OF APPLICABLE LAWS. IN NO EVENT SHALL THE DEVELOPER BE HELD LIABLE FOR SPECIAL COLLATERAL, INCIDENTAL OR CONSEQUENTIAL LIABILITY IN CONNECTION WITH THE USE OF THIS DIGITAL DATA ONCE RELEASED FROM THE DEVELOPER'S OFFICE. THIS DRAWING IS TO BE READ & UNDERSTOOD IN CONJUNCTION WITH THE STRUCTURAL, MECHANICAL, ELECTRICAL & / OR ANY OTHER CONSULTANT'S DOCUMENTATION AS MAY BE APPLICABLE TO THE PROJECT PRIOR TO THE START OF ANY WORKS AND FOR ITS DURATION.


PROJECT:
Residential Building
LOT 10 IN DP 263073
No.17 ADAM PLACE MACQUARIE
FIELDS NSW 2564

DRAWING TITLE:
**WATERPROOFING
NOTES**

NORTH:


LOT NO:	DATE:	SCALE:	DRAWING No:	REV:
10	21-07-2026	1 : 50	CC.17	11
DRAWN BY:	CHECKED BY:	ISSUED BY:		
AS	RH			
DRAFTED BY:	CLIENT NAME:			
ROHIT	Anila Gurung & Amodh Gurung			

CC ISSUE

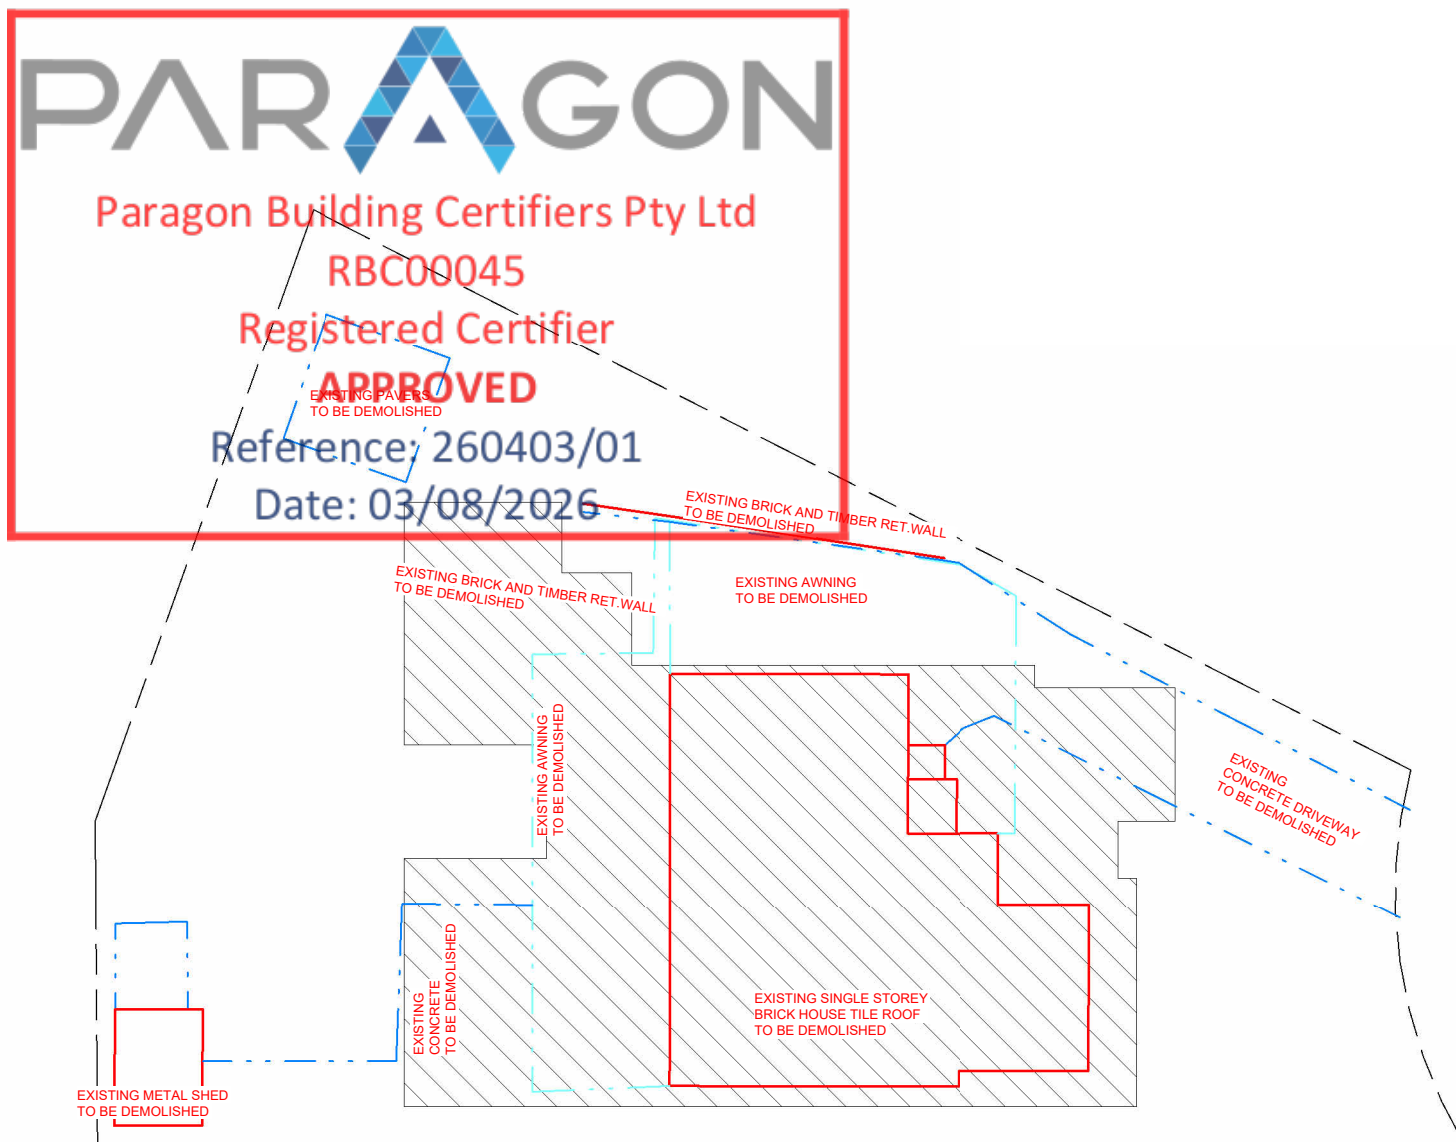

1 DEMOLITION PLAN
1 : 200

NOTES:

Location of stockpile material & waste i.e. bricks, tiles & similar materials timber offcuts & recycleable materials & waste for landfill top soil sand stockpile to be covered and protected with geotextile fabric.

Vehicles carrying loose building materials to be covered in compliance with road traffic regulations, safe access for heavy equipment plant & material delivery.

Demolish & remove from the site as per the specification the council requirement & AS260-2001. All the existing buildings, carport, fences, driveway paths, and the like as shown dotted and or as required to achieve the proposed work, redundant services prior to demolition.

Provide 1800 mm high safety & security fence for the duration of the demolition & construction works silt fence, geotextile fabric or the equivalent to all boundaries.

Method of support of excavation adjacent to adjoining properties to engineer's details and it is to be certified by a certificate accredited in civil engineering.

Any damage to existing and/or adjoining property and/or services to be made good with minimal if any inconvenience to all properties, if any damage due to negligence, it is to be reflected at the cost of the negligent party which caused that damage.

Sediment controls to be placed access driveway.

Provide 1800 mm high access gate with padlock.

- EXISTING BUILDING TO BE DEMOLISHED
- EXISTING ROOF TO BE DEMOLISHED
- EXISTING AWNING TO BE DEMOLISHED
- EXISTING DRIVEWAY TO BE DEMOLISHED
- EXISTING GARDEN TO BE DEMOLISHED
- PROPOSED 2 STOREY BUILDING
- TREE TO BE removed

				CC ISSUE								
				 THIS DRAWING IS THE EXCLUSIVE PROPERTY OF THE DEVELOPER & THE REPRODUCTION OF ANY PART WITHOUT THE PRIOR WRITTEN CONSENT OF THE DEVELOPER IS A VIOLATION OF APPLICABLE LAWS. IN NO EVENT SHALL THE DEVELOPER BE HELD LIABLE FOR SPECIAL COLLATERAL, INCIDENTAL OR CONSEQUENTIAL LIABILITY IN CONNECTION WITH THE USE OF THIS DIGITAL DATA ONCE RELEASED FROM THE DEVELOPER'S OFFICE. THIS DRAWING IS TO BE READ & UNDERSTOOD IN CONJUNCTION WITH THE STRUCTURAL, MECHANICAL, ELECTRICAL & / OR ANY OTHER CONSULTANT'S DOCUMENTATION AS MAY BE APPLICABLE TO THE PROJECT PRIOR TO THE START OF ANY WORKS AND FOR ITS DURATION.	PROJECT: Residential Building LOT 10 IN DP 263073 No.17 ADAM PLACE MACQUARIE FIELDS NSW 2564	DRAWING TITLE: DEMOLITION PLAN	NORTH: 	LOT NO: 10	DATE: 21-07-2026	SCALE: As indicated	DRAWING No: CC.19	REV: 11
								DRAWN BY: ROHIT	CHECKED BY: RH		ISSUED BY:	
11	17-04-2026	DA ISSUE										
10	26-03-2026	Rendered Pillar and Porch cover with only flashing added - Ekta										
7	26-02-2026	Bank Set										
REV	DATE	DESCRIPTION	BY					DRAFTED BY: ROHIT	CLIENT NAME: Anila Gurung & Amodh Gurung			

ACBC HOUSING PROVISIONS : PART 9.3 FIRE SEPARATION OF EXTERNAL WALLS

9.3.1 SEPARATING WALLS

- (1) A SEPARATING WALL BETWEEN CLASS 1 BUILDINGS, OR A WALL THAT SEPARATE A CLASS 1 BUILDING FROM A CLASS 10A BUILDING WHICH IS NOT ASSOCIATED WITH THE CLASS 1 BUILDING MUST -
- (A) BE CONSTRUCTED -
- (I) HAVING AN FRL OF NOT LESS THAN 60/60/60; OR
- (II) OF MASONRY NOT LESS THAN 90MM THICK; AND
- (B) COMMENCE AT THE FOOTINGS OR GROUND SLAB (SEE FIGURE 9.3.1A), EXCEPT FOR HORIZONTAL PROJECTIONS TO WHICH 9.3.4 APPLIES (SEE FIGURE 9.3.4); AND
- (C) EXTEND -
- (I) IF THE BUILDING HAS A NON-COMBUSTIBLE ROOF COVERING, TO THE UNDERSIDE OF THE ROOF COVERING (SEE FIGURE 9.3.1A AND FIGURE 9.3.1B); OR
- (II) IF THE BUILDING HAS A COMBUSTIBLE ROOF COVERING, TO NOT LESS THAN 450MM ABOVE THE ROOF COVERING (SEE FIGURE 9.3.1A); AND
- (D) COMPLY WITH (2) TO (5) AND 9.3.2 AS APPLICABLE
- (2) A SEPARATING WALL OF LIGHTWEIGHT CONSTRUCTION MUST BE TESTED IN ACCORDANCE WITH SPECIFICATION 6.
- (3) A SEPARATING WALL COMPLYING WITH (1)(C)(I) -
- (A) MUST NOT BE CROSSED BY TIMBER OR OTHER COMBUSTIBLE BUILDING ELEMENTS EXCEPT FOR ROOF BATTENS WITH DIMENSIONS OF 75 X 50 MM OR LESS, OR ROOF SARKING; AND
- (B) MUST HAVE ANY GAP BETWEEN THE TOP OF THE WALL AND THE UNDERSIDE OF THE ROOF COVERING PACKED WITH MINERAL FIBRE OR OTHER SUITABLE FIRE-RESISTING MATERIAL.
- (4) WHERE A BUILDING HAS A MASONRY VENEER EXTERNAL WALL, ANY GAP BETWEEN THE SEPARATING WALL AND THE EXTERNAL MASONRY VENEER MUST BE -
- (A) NOT MORE THAN 50 MM; AND
- (B) PACKED WITH A MINERAL FIBRE OR OTHER SUITABLE FIRE-RESISTING MATERIAL WITH THE PACKING ARRANGED TO MAINTAIN ANY WEATHERPROOFING REQUIREMENTS OF HDB4.
- (5) EAVES, VERANDAHS AND SIMILAR SPACES THAT ARE OPEN TO THE ROOF SPACE AND ARE COMMON TO MORE THAN ONE CLASS 1 DWELLING MUST BE SEPARATING BY A NON-COMBUSTIBLE VERTICAL LINING (SEE FIGURE 9.3.1C)

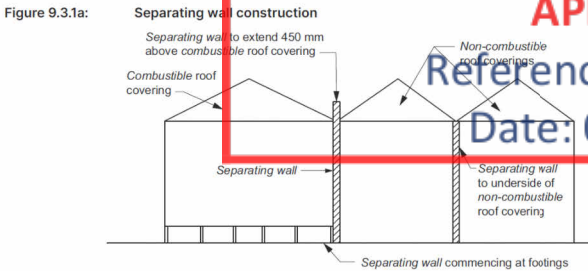


Figure 9.3.1b: Separating wall construction — Underside of non-combustible roof cladding (diagram 1)

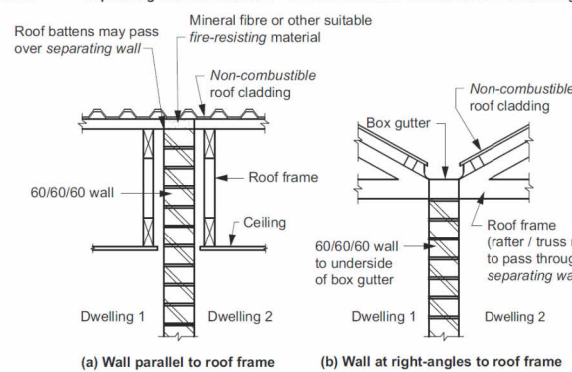


Figure 9.3.1c: Separating wall construction — Underside of non-combustible roof cladding (diagram 2)


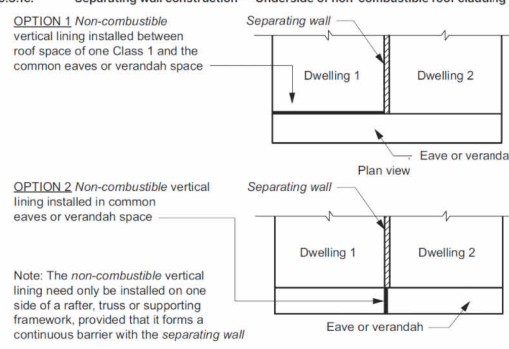


Figure 9.3.4: Horizontal projection forming part of a separating wall

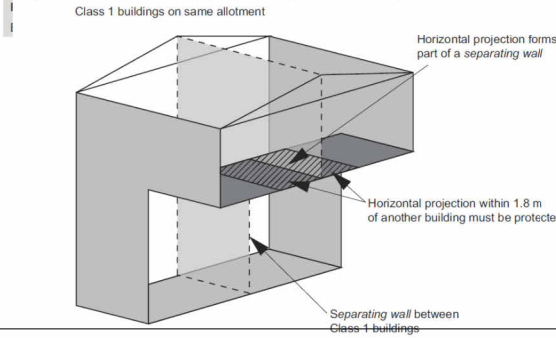

9.3.2 SERVICES IN SEPARATING WALLS

- (1) ANY SERVICE OPENING, OTHER THAN THOSE LISTED IN (2), (3) AND (4), IN A SEPARATING WALL MUST HAVE CONSTRUCTION WITH AN FRL OF NOT LESS THAN -/60/60.
- (2) IF AN ELECTRICAL WIRE OR CABLE PENETRATES A SEPARATING WALL -
- (A) THE SERVICE AND BUILDING ELEMENT AT THE PENETRATION MUST -
- (I) BE IDENTICAL WITH A PROTOTYPE ASSEMBLY THAT HAS BEEN TESTED IN ACCORDANCE WITH AS 4072.1 AND AS 1530.4 AND ACHIEVE AN FRL OF NOT LESS THAN -/60/60; OR
- (II) DIFFER FROM A PROTOTYPE ASSEMBLY OF THE SERVICE AND BUILDING ELEMENT IN ACCORDANCE WITH 4072.1; OR
- (B) THE SERVICE MUST BE INSTALLED SO THAT -
- (I) THE OPENING IS NEATLY FORMED, CUT OR DRILLED AND NO CLOSER THAN 50 MM TO ANY OTHER SERVICE; AND
- (II) THE OPENING IS NO LARGER IN CROSS-SECTION THAN -
- (A) 2000 MM² IF ONLY A SINGLE CABLE IS ACCOMMODATED AND THE GAP BETWEEN THE CABLE AND THE WALL IS NO WIDER THAN 15MM; OR
- (B) 500 MM² IN ANY OTHER CASE; AND
- (III) ANY GAP BETWEEN THE SERVICE AND THE WALL IS PACKED WITH MINERAL FIBRE OR OTHER SUITABLE FIRE-RESISTING MATERIAL.
- (3) IF AN ELECTRICAL SWITCH, OUTLET, SOCKET OR THE LIKE IS ACCOMMODATED IN A SEPARATING WALL -
- (A) THE SERVICE AND BUILDING ELEMENT AT THE PENETRATION MUST -
- (I) BE IDENTICAL WITH A PROTOTYPE ASSEMBLY WHICH HAS BEEN TESTED IN ACCORDANCE WITH AS 4072.1 AND AS 1530.4 AND ACHIEVE AN FRL OF NOT LESS THAN -/60/60; OR
- (II) DIFFER FROM A PROTOTYPE ASSEMBLY OF THE SERVICE AND BUILDING ELEMENT IN ACCORDANCE WITH AS 4072.1; OR
- (B) THE SERVICE MUST BE INSTALLED SO THAT -
- (I) THE OPENING OR RECESS -
- (A) IS NOT LOCATED OPPOSITE ANY POINT WITHIN 300MM HORIZONTALLY OR 600MM VERTICALLY OF ANY OPENING OR RECESS ON THE OPPOSITE SIDE OF THE WALL; OR
- (B) DOES NOT EXTEND BEYOND HALF THE THICKNESS OF THE WALL; AND
- (II) ANY GAP BETWEEN THE SERVICE AND THE WALL IS PACKED WITH MINERAL FIBRE OR OTHER SUITABLE FIRE-RESISTING MATERIAL.
- (4) OTHER THAN WHERE A TESTED SYSTEM IS USED IN ACCORDANCE WITH (3)(A), IF AN ELECTRICAL SWITCH, SOCKET, OUTLET OR THE LIKE IS ACCOMMODATED IN A HOLLOW SEPARATING WALL, THE CAVITY IMMEDIATELY BEHIND THE SERVICE MUST BE FRAMED AND PACKED WITH MINERAL FIBRE OR SUITABLE FIRE-RESISTING MATERIAL (SEE FIGURE 9.3.2).

9.3.3 ROOF LIGHTS

- COMBUSTIBLE ROOF LIGHTS, SKYLIGHTS OR THE LIKE INSTALLED IN A ROOF OR PART OF A ROOF REQUIRED TO HAVE A NON-COMBUSTIBLE COVERING MUST -
- (A) HAVE AN AGGREGATE AREA NOT MORE THAN 20% OF THE ROOF OR PART OF THE ROOF; AND
- (B) BE NOT LESS THAN 900MM FROM THE VERTICAL PROJECTION OF A SEPARATING WALL EXTENDING TO THE UNDERSIDE OF THE ROOF COVERING.

9.3.4 HORIZONTAL PROJECTIONS

- (1) WHERE A HORIZONTAL PROJECTION FORMS PART OF A SEPARATING WALL COMPLYING WITH 9.3.1, ANY HORIZONTAL PROJECTION WITHIN 1.8M ON EACH SIDE OF THE SEPARATING WALL (SEE FIGURE 9.3.4) MUST -
- (A) BE A FLOOR/CEILING OR FLOOR/SOFFIT SYSTEM INCORPORATING A CEILING OR SOFFIT WHICH HAS A RESISTANCE TO THE INCIDENT SPREAD OF FIRE TO THE SPACE ABOVE ITSELF OF NOT LESS THAN 60 MINUTES; OR
- (B) HAVE AN FRL NOT LESS THAN 30/30/30 WHEN TESTED FROM THE UNDERSIDE; OR
- (C) HAVE A FIRE-PROTECTIVE COVERING ON THE UNDERSIDE OF THE FLOOR, INCLUDING BEAMS INCORPORATED IN IT, IF THE FLOOR IS COMBUSTIBLE OR OF METAL.
- (2) THE PART OF THE SEPARATING WALL THAT PROJECTS OUTWARDS HORIZONTALLY MUST -
- (A) EXTEND TO THE UNDERSIDE OF THE FLOOR/CEILING OR FLOOR/SOFFIT SYSTEM COMPLYING WITH (1); AND
- (B) NOT BE CROSSED BY TIMBER OR OTHER COMBUSTIBLE BUILDING ELEMENTS EXCEPT FOR FRAMING MEMBERS WITH DIMENSIONS OF 75 X 50MM OR LESS, OR SARKING; AND
- (C) HAVE ANY GAP BETWEEN THE BOTTOM OF THE WALL AND THE UNDERSIDE OF THE FLOOR/CEILING OR FLOOR/SOFFIT SYSTEM PACKED WITH MINERAL FIBRE OR OTHER SUITABLE FIRE-RESISTING MATERIAL.
- (3) WHERE A FLOOR SUBJECT TO (1)(B) DEPENDS ON DIRECT VERTICAL OR LATERAL SUPPORT FROM ANOTHER PART TO MAINTAIN ITS FRL, THAT SUPPORTING PART MUST HAVE AN FRL OF NOT LESS THAN 30/-.
- (4) WHERE A SERVICE PASSES THROUGH A FLOOR REFERRED TO IN (1), THE PENETRATION MUST NOT REDUCE THE FIRE PERFORMANCE OF THE FLOOR OR COVERING.

Figure 10.7.1: Required airborne and impact sound insulation — Plan view



Figure 10.7.2a: Sound insulation between buildings — Stud wall junctions

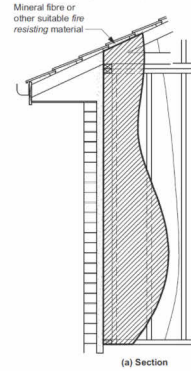


Figure 10.7.5a: Two leaves of 110 mm clay brick masonry (method 1)

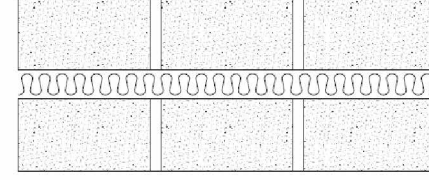


Figure 10.7.5b: Two leaves of 110 mm clay brick masonry (method 2)


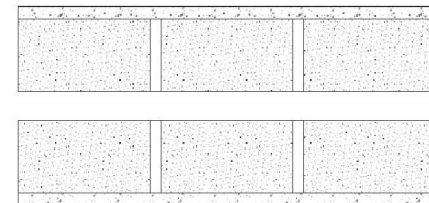


Figure 10.7.5c: Single leaf of 110 mm clay brick masonry

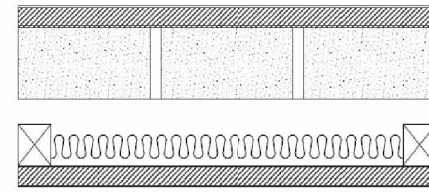

ACBC HOUSING PROVISIONS : PART 10.7 SOUND INSULATION

10.7.1 SOUND INSULATION

- (1) A SEPARATING WALL BETWEEN CLASS 1 BUILDINGS, OR A WALL THAT SEPARATES A CLASS 1 BUILDING FROM A CLASS 10A BUILDING WHICH IS NOT ASSOCIATED WITH THE CLASS 1 BUILDING MUST -
- (A) HAVE AN $R_w + C_{tr}$ (AIRBORNE) NOT LESS THAN 50; AND
- (B) BE OF DISCONTINUOUS CONSTRUCTION IF IT SEPARATES A BATHROOM, SANITARY COMPARTMENT, LAUNDRY OR KITCHEN IN ONE CLASS 1 BUILDING (SEE FIGURE 10.7.1)
- (2) A WALL REQUIRED TO HAVE SOUND INSULATION MUST CONTINUE TO -
- (A) THE UNDERSIDE OF THE ROOF ABOVE; OR
- (B) A CEILING THAT PROVIDES THE SOUND INSULATION REQUIRED FOR THE WALL.

10.7.2 DETERMINATION OF AIRBORNE SOUND INSULATION RATINGS

- THE $R_w + C_{tr}$ SOUND INSULATION RATING REQUIRED BY 10.7.1(1)(A) MUST -
- (A) BE DETERMINED IN ACCORDANCE WITH AS/NZS ISO 717.1, USING RESULTS FROM LABORATORY MEASUREMENTS; OR
- (B) COMPLY WITH 10.7.5 TO 10.7.8 AND THE RELEVANT PROVISIONS OF 10.7.3.

10.7.3 CONSTRUCTION OF SOUND INSULATED WALLS

- TO ACHIEVE THE APPROPRIATE LEVEL OF SOUND INSULATION, WALLS MUST BE CONSTRUCTED AS FOLLOWS:
- (A) STUD WALL JUNCTION - JUNCTIONS OF SOUND INSULATED WALLS WITH ANY PERIMETER WALLS AND ROOF CLADDING MUST BE SEALED IN ACCORDANCE WITH FIGURE 10.7.3A.
- (B) MASONRY - UNITS MUST BE LAID WITH ALL JOINTS FILLED SOLID, EXCEPT FOR ARTICULATION JOINTS COMPLYING WITH 5.6.8, INCLUDING THOSE BETWEEN THE MASONRY AND ANY ADJOINING CONSTRUCTION.
- (C) CONCRETE PANELS - MUST HAVE JOINTS BETWEEN PANELS AND ANY ADJOINING CONSTRUCTION FILLED SOLID.
- (D) PLASTERBOARD SHEETING -
- (I) IF TWO LAYERS ARE REQUIRED, THE SECOND LAYER JOINTS MUST NOT COINCIDE WITH THOSE OF THE FIRST LAYER (SEE FIGURE 10.7.3B).
- (II) JOINTS BETWEEN SHEETS INCLUDING THE OUTER LAYER OR BETWEEN SHEETS AND ANY ADJOINING CONSTRUCTION MUST BE TAPED AND FILLED SOLID.
- (E) STEEL FRAMED CONSTRUCTION - STEEL FRAMING AND PERIMETER MEMBERS MUST BE INSTALLED AS FOLLOWS:
- (I) STEEL FRAMING MEMBERS MUST BE NOT LESS THAN 0.6MM THICK.
- (II) STUDS MUST BE NOT LESS THAN 63MM IN DEPTH UNLESS ANOTHER DEPTH IS SPECIFIED IN 10.7.5 TO 10.7.8.
- (F) TIMBER-FRAMED CONSTRUCTION - TIMBER STUDS AND PERIMETER MEMBERS MUST BE INSTALLED AS FOLLOWS:
- (I) NOGGINGS AND LIKE MEMBERS MUST NOT BRIDGE BETWEEN STUDS SUPPORTING DIFFERENT WALL LEAVES.
- (II) ALL TIMBER MEMBERS AT THE PERIMETER OF THE WALL MUST BE SECURELY FIXED TO THE ADJOINING STRUCTURE AND THE JOINTS MUST BE CAULKED SO THERE ARE NO VOIDS BETWEEN THE TIMBER MEMBERS AND THE WALL.

10.7.4 SERVICES

- (1) SERVICES MUST NOT BE CHASED INTO CONCRETE OR MASONRY SEPARATING WALLS.
- (2) IF A DUCT, SOIL, WASTE, WATER SUPPLY OR STORMWATER PIPE IS LOCATED IN A SEPARATING WALL -
- (A) A DOOR OR PANEL PROVIDING ACCESS TO A DUCT OR PIPE REQUIRED TO BE SEPARATED MUST -
- (I) NOT OPEN INTO ANY HABITABLE ROOM, OTHER THAN KITCHEN; AND
- (II) IN ANY OTHER PART MUST BE FIRMLY FIXED SO AS TO OVERLAP THE FRAME OR REBATE OF THE FRAME BY NOT LESS THAN 10 MM AND BE CONSTRUCTED OF -
- (A) WOOD, PLASTERBOARD OR BLOCKBOARD NOT LESS THAN 33MM THICK; OR
- (B) COMPRESSED FIBRE REINFORCED CEMENT SHEETING NOT LESS THAN 9MM THICK; OR
- (C) OTHER SUITABLE MATERIAL WITH A MASS PER UNIT AREA NOT LESS THAN 24.4 KG/M²; AND
- (B) IN THE CASE OF A WATER SUPPLY PIPE, IT MUST -
- (I) ONLY BE INSTALLED IN DISCONTINUOUS CONSTRUCTION; AND
- (II) IN THE CASE OF A WATER SUPPLY PIPE THAT SERVES ONE DWELLING, NOT BE FIXED TO THE WALL LEAF ON THE SIDE OF ANY OTHER DWELLING AND HAVE A CLEARANCE NOT LESS THAN 10 MM TO THE OTHER WALL LEAF.
- (3) ELECTRICAL OUTLETS MUST BE OFFSET FROM EACH OTHER -
- (A) IN MASONRY WALLING, NOT LESS THAN 100MM; AND
- (B) IN TIMBER OR STEEL-FRAMED WALLING, NOT LESS THAN 300MM.

10.7.5 ACCEPTABLE FORMS OF CONSTRUCTION FOR MASONRY WALLS

- (1) ACCEPTABLE FORMS OF CONSTRUCTION FOR MASONRY WALLS ARE SET OUT IN (2) TO (6).
- (2) TWO LEAVES OF 110MM CLAY BRICK MASONRY WITH -
- (A) A CAVITY NOT LESS THAN 50MM BETWEEN LEAVES; AND
- (B) 50MM THICK GLASS WOOL INSULATION WITH A DENSITY OF 11 KG/M³ OR 50MM THICK POLYESTER INSULATION WITH A DENSITY OF 20 KG/M³ IN THE CAVITY,
- HAS AN $R_w + C_{tr}$ OF NOT LESS THAN 50, IF CONSTRUCTED IN ACCORDANCE WITH FIGURE 10.7.5A.
- (3) TWO LEAVES OF 110MM CLAY BRICK MASONRY WITH -
- (A) A CAVITY NOT LESS THAN 50MM BETWEEN LEAVES; AND
- (B) 13MM CEMENT RENDER ON EACH OUTSIDE FACE,
- HAS AN $R_w + C_{tr}$ OF NOT LESS THAN 50, IF CONSTRUCTED IN ACCORDANCE WITH FIGURE 10.7.5B.
- (4) A SINGLE LEAF OF 110 MM CLAY BRICK MASONRY WITH -
- (A) A ROW OF 70MMX35MM TIMBER STUDS OR 64 MM STEEL STUDS AT 600MM CENTERS, SPACED 20MM FROM THE MASONRY WALL; AND
- (B) 50MM THICK MINERAL INSULATION OR GLASS WOOL INSULATION WITH A DENSITY OF 11 KG/M³ POSITIONED BETWEEN STUDS; AND
- (C) ONE LAYER OF 13MM PLASTERBOARD FIXED TO OUTSIDE FACE OF STUDS AND OUTSIDE FACE OF MASONRY,
- HAS AN $R_w + C_{tr}$ OF NOT LESS THAN 50, IF CONSTRUCTED IN ACCORDANCE WITH FIGURE 10.7.5C.
- (5) A SINGLE LEAF OF 90MM CLAY BRICK MASONRY WITH -
- (A) A ROW OF 70MM X 35MM TIMBER STUDS OR 64 MM STEELS STUDS AT 600MM CENTRES, SPACED 20MM FROM EACH FACE OF THE MASONRY WALL; AND
- (B) 50MM THICK MINERAL INSULATION OR GLASS WOOL INSULATION WITH A DENSITY OF 11 KG/M³ POSITIONED BETWEEN STUDS IN EACH ROW; AND
- (C) ONE LAYER OF 13MM PLASTERBOARD FIXED TO STUDS ON EACH OUTSIDE FACE, HAS AN $R_w + C_{tr}$ OF NOT LESS THAN 50, IF CONSTRUCTED IN ACCORDANCE WITH FIGURE 10.7.5D.
- (6) A SINGLE LEAF OF 220 MM BRICK MASONRY WITH 13MM CEMENT RENDER ON EACH FACE HAS AN $R_w + C_{tr}$ OF NOT LESS THAN 50, IF CONSTRUCTED IN ACCORDANCE WITH FIGURE 10.7.5E

Figure 10.7.5d: Single leaf of 90 mm clay brick masonry


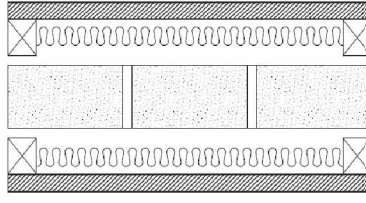


Figure 10.7.5e: Single leaf of 220 mm brick masonry with 13 mm cement render on each face



CC ISSUE

REV	DATE	DESCRIPTION	BY
11	17-04-2026	DA ISSUE	
10	26-03-2026	Rendered Pillar and Porch cover with only flashing added - Ekta	
7	26-02-2026	Bank Set	

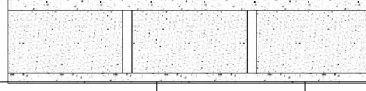


RUBY HOMES

THIS DRAWING IS THE EXCLUSIVE PROPERTY OF THE DEVELOPER & THE REPRODUCTION OF ANY PART WITHOUT THE PRIOR WRITTEN CONSENT OF THE DEVELOPER IS A VIOLATION OF APPLICABLE LAWS. IN NO EVENT SHALL THE DEVELOPER BE HELD LIABLE FOR SPECIAL COLLATERAL, INCIDENTAL OR CONSEQUENTIAL LIABILITY IN CONNECTION WITH THE USE OF THIS DIGITAL DATA ONCE RELEASED FROM THE DEVELOPER'S OFFICE. THIS DRAWING IS TO BE READ & UNDERSTOOD IN CONJUNCTION WITH THE STRUCTURAL, MECHANICAL, ELECTRICAL & / OR ANY OTHER CONSULTANT'S DOCUMENTATION AS MAY BE APPLICABLE TO THE PROJECT PRIOR TO THE START OF ANY WORKS AND FOR ITS DURATION.

PROJECT:
Residential Building
LOT 10 IN DP 263073
No.17 ADAM PLACE MACQUARIE
FIELDS NSW 2564

DRAWING TITLE:
**SEPARATING WALL
DETAILS**

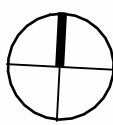NORTH:


LOT NO: 10	DATE: 21-07-2026	SCALE: 1 : 50	DRAWING No: CC.20	REV: 11
DRAWN BY: AS	CHECKED BY: RH			ISSUED BY:
DRAFTED BY: SL	CLIENT NAME: Anila Gurung & Amodh Gurung			