

LOT 124 - 45 MERIDIAN STREET, LEPPINGTON. IN DP 1299327.
PROPOSED CONSTRUCTION OF A TWO STOREY DWELLING



BASIS COMMITMENTS	
WATER	
LANDSCAPE	70m2
TOILETS	4 STARS
KITCHEN TAPS	4 STARS
SHOWER HEADS	4 STAR (>4.5 but <=6 Umin)
BASIN TAPS	4 STARS
ALTERNATIVE WATER	1500L RAINWATER TANK
ROOF WATER TO TANK	206m2
ALT.WATER USES- TANK	LAUNDRY
ALT. WATER USES - RETIC	ALL TOILETS + ONE OUTDOOR TAP
SWIMMING POOL	N/A
ENERGY	
HOT WATER	GAS INSTANTANEOUS - 5 STAR
AIR-CON (HEATING)	3 PHASE DUCTED - EER 3.0-3.5
AIR-CON (COOLING)	3 PHASE DUCTED - EER 3.0-3.5
VENTILATION - BATHROOM	NONE/ NATURAL VENTILATION
VENTILATION - KITCHEN	DUCTED - MANUAL SWITCH
VENTILATION - LAUNDRY	NONE/ NATURAL VENTILATION
PV SYSTEM	N/A
COOKTOP	GAS
OVEN	ELECTRIC
CLOTHES DRYING	OUTDOOR CLOTHESLINE
LIGHTING	DEDICATED LED

OnBuild Certifiers Pty Ltd

Reference: 260043
GENERAL LEGEND
Date: 03/08/2020

AC	AIR CONDITIONING UNIT
AL	POWDER COATED ALUMINIUM DOOR
BAL	BALUSTRADE RAIL
BDC2940	
BG	BOX GUTTER
CAR	CARPENTRY, CARPENTRY AND JOINERY
CAR	METAL CAPPING

Consultant work preparation document
number: 16500008
is responsible for accuracy

AC	AIR CONDITIONING UNIT
AL	POWDER COATED ALUMINIUM DOOR/ WINDOW
BA	BALUSTRADE TYPE
BG	BDC2940 BOX GUTTER
CB	CERAMIC TILE
CD	CEMENT CAPPING
CD1, CD2, etc.	WALL CLADDING
CONC.	CONCRETE FLOOR
CPT	CARPET
CRT	CONCRETE ROOF TILES
CR1, CR2, etc.	CEMENT RENDER TYPE/ COLOUR
DP/S	DOWN PIPE
DW	DISH WASHER
ED	ENTRY DOOR
F	FRIDGE
FAS	FASCIA
FET	FEATURE TILE
FT, FT1, FT2, etc.	FLOOR TILES
FW	FLOOR WASTE
GD	GARAGE DOOR
GUT	GUTTER
HWU	HOT WATER UNIT
HYB	HYBRID FLOOR
L	LINEN
MR	METAL ROOF
MW	MICROWAVE OVEN
NGL	NATURAL GROUND LEVEL
OBS	OBSCURED GLASS
P	PANTRY
R	ROBE
RL	REDUCED LEVEL
RWH	RAIN WATER HEAD
RWT	RAIN WATER TANK
S	STORAGE
TOW	TOP OF WALL
TL	TIMBER LAMINATE
WC	WATER CLOSET
WM	WASHING MACHINE
SD	SMOKE DETECTOR

Sheet List				
Sheet No.	Sheet Name	Drawn By	Current Revision Date	Current Revision
CDC.01	COVER SHEET	AS	12-06-2026	CDC ISSUE
CDC.02A	GENERAL NOTES	AS	12-06-2026	CDC ISSUE
CDC.02B	GENERAL NOTES	AS	12-06-2026	CDC ISSUE
CDC.03	LOCATION PLAN AND SITE PLAN	AS	12-06-2026	CDC ISSUE
CDC.04	SITE ANALYSIS AND SEDIMENT CONTROL	AS	12-06-2026	CDC ISSUE
CDC.05	GROUND FLOOR PLAN	AS	12-06-2026	CDC ISSUE
CDC.06	FIRST FLOOR LEVEL	AS	12-06-2026	CDC ISSUE
CDC.07	ROOF PLAN	AS	12-06-2026	CDC ISSUE

Sheet List				
Sheet No.	Sheet Name	Drawn By	Current Revision Date	Current Revision
CDC.08	ELEVATION 01	AS	12-06-2026	CDC ISSUE
CDC.09	ELEVATION 02	AS	12-06-2026	CDC ISSUE
CDC.10	SECTIONS	AS	12-06-2026	CDC ISSUE
CDC.11	FLOOR AREA PLAN	AS	12-06-2026	CDC ISSUE
CDC.12	RENTABLE AREA PLAN	AS	12-06-2026	CDC ISSUE
CDC.14	COLOR SCHEDULE	AS	12-06-2026	CDC ISSUE
CDC.15	LANDSCAPE PLAN	AS	12-06-2026	CDC ISSUE
CDC.16	WATERPROOFING DETAILS	AS	12-06-2026	CDC ISSUE

3	12-06-2026	Area increased	
2	10-06-2026	Building flipped as per WAE, 230 brick wall in Garage, Garage slope made 5 degrees	
1	13-03-2026	Bank Set	
REV	DATE	DESCRIPTION	BY



THIS DRAWING IS THE EXCLUSIVE PROPERTY OF THE DEVELOPER & THE REPRODUCTION OF ANY PART WITHOUT THE PRIOR WRITTEN CONSENT OF THE DEVELOPER IS A VIOLATION OF APPLICABLE LAWS. NO EVENT SHALL THE DEVELOPER BE HELD LIABLE FOR SPECIAL, COLLATERAL, INCIDENTAL OR CONSEQUENTIAL LIABILITY IN CONNECTION WITH THE USE OF THIS DIGITAL DATA ONCE RELEASED FROM THE DEVELOPER'S OFFICE. THIS DRAWING IS TO BE READ & UNDERSTOOD IN CONJUNCTION WITH THE STRUCTURAL, MECHANICAL, ELECTRICAL & / OR ANY OTHER CONSULTANT'S DOCUMENTATION AS MAY BE APPLICABLE TO THE PROJECT PRIOR TO THE START OF ANY WORKS AND EFFORTS DURATION.

PROJECT:
LOT 124

45 MERIDIAN STREET,
LEPPINGTON

DRAWING TITLE:
COVER SHEET

NORTH:

LOT NO:	124
---------	-----

DRAWN BY
AS

DRAFTED BY
ID

DATE:	27-07-2026
-------	------------

7.	CHECKED BY:
	RH

CLIENT NAME:	Owner
--------------	-------

SCALE:

indicated

CDC ISSUE

<u>DRAWING</u> <u>No:</u>	<u>REV:</u> 3
------------------------------	---------------

CDC.01	ISSUED BY:
---------------	------------

BUILDING SPECIFICATIONS

National Construction Code – Volume 2, Amendment 1 – Building Code of Australia 2022 & Housing Provisions Standard 2022

SITE PREPARATION

- PART 3.1 OF THE NCC VOLUME 2, AMENDMENT 1 - BUILDING CODE OF AUSTRALIA 2022 & HOUSING PROVISIONS STANDARD 2022.

EARTHWORKS

- TO BE CARRIED OUT IN ACCORDANCE WITH THE REQUIREMENTS OF THE ENVIRONMENTAL PLANNING & ASSESSMENT ACT 1979 AND DEVELOPMENT CONSENT CONDITIONS
- PART 3.2 OF THE NCC VOLUME 2, AMENDMENT 1 - BUILDING CODE OF AUSTRALIA 2022 & HOUSING PROVISIONS STANDARD 2022.
- AS 4678:2002 - EARTH-RETAINING STRUCTURES

DRAINAGE

- PART 3.3 OF THE NCC VOLUME 2, AMENDMENT 1 - BUILDING CODE OF AUSTRALIA 2022 & HOUSING PROVISIONS STANDARD 2022.
- AS/NZS 3500.1:2021 - PLUMBING & DRAINAGE - WATER SERVICES
- AS/NZS 3500.2:2021 - PLUMBING & DRAINAGE - SANITARY PLUMBING & DRAINAGE
- AS/NZS 3500.3:2021 - PLUMBING & DRAINAGE STORMWATER DRAINAGE
- AS/NZS 3500.4:2021 - PLUMBING & DRAINAGE - HEATED WATER SERVICES

STRUCTURAL WORK

- Part 2.2 OF THE NCC VOLUME 2, AMENDMENT 1 - BUILDING CODE OF AUSTRALIA 2022 & HOUSING PROVISIONS STANDARD 2022.
- AS 4100:2020- STEEL STRUCTURES CODES
- AS/NZS 1170.0:2002 – GENERAL PRINCIPLES
- AS/NZS 1170.1:2002 – PARTS 1 PERMANENT, IMPOSED AND OTHER ACTIONS
- AS/NZS 1170.2:2021 – PART 2 WIND ACTIONS
- AS 3700:2018– SAA MASONRY CODE
- AS 1684.3:2021- RESIDENTIAL TIMBER FRAMED CONSTRUCTION

FOOTINGS & SLABS

- PART 4 OF THE NCC VOLUME 2, AMENDMENT 1 - BUILDING CODE OF AUSTRALIA 2022 & HOUSING PROVISIONS STANDARD 2022.
- AS 2159:2009 - PILING - DESIGN & INSTALLATION
- AS 2870:2011 - RESIDENTIAL SLABS & FOOTINGS
- AS 3600:2018 - CONCRETE STRUCTURES

MASONRY

- PART 5 OF THE NCC VOLUME 2, AMENDMENT 1 - BUILDING CODE OF AUSTRALIA 2022 & HOUSING PROVISIONS STANDARD 2022.
- AS 3700:2018 - MASONRY STRUCTURES

FRAMING

- PART 6 OF THE NCC VOLUME 2, AMENDMENT 1 - BUILDING CODE OF AUSTRALIA 2022 & HOUSING PROVISIONS STANDARD 2022.
- AS 1684.2:2021 - RESIDENTIAL TIMBER-FRAMED CONSTRUCTION - NON- CYCLONIC AREAS
- AS 1720.1:2010 - TIMBER STRUCTURES - DESIGN METHODS
- AS 4100:2020 - STEEL STRUCTURES
- AS 3660.1:2014 – TERMITE MANAGEMENT SYSTEM

ROOF & WALL CLADDING

- PART 7 OF THE NCC VOLUME 2, AMENDMENT 1 - BUILDING CODE OF AUSTRALIA 2022 & HOUSING PROVISIONS STANDARD 2022.
- AS 1273:1991 - UNPLASTICIZED PVC (UPVC) DOWNPIPES & FITTINGS FOR RAINWATER
- AS 1562.1:2018 - DESIGN & INSTALLATION OF SHEET ROOF & WALL CLADDING - METAL
- AS/NZS 1562.3:2006 - DESIGN & INSTALLATION OF SHEET ROOF & WALL CLADDING - PLASTIC
- AS 2049:2002 - ROOF TILES
- AS 2050:2018 - INSTALLATION OF ROOF TILES
- AS 4285:2019 – ROOFLIGHTS

GLAZING

- PART 8 OF THE NCC VOLUME 2, AMENDMENT 1 - BUILDING CODE OF AUSTRALIA 2022 & HOUSING PROVISIONS STANDARD 2022.
- AS 1288:2021 - GLASS IN BUILDINGS - SELECTION & INSTALLATION
- AS 2047:2014 - WINDOWS & EXTERNAL GLAZED DOORS IN BUILDINGS
- AS/NZS 2208:1996 - SAFETY GLAZING MATERIALS IN BUILDINGS

FIRE SAFETY

- PART 9 OF THE NCC VOLUME 2, AMENDMENT 1 - BUILDING CODE OF AUSTRALIA 2022 & HOUSING PROVISIONS STANDARD 2022.
- AS 3786:2014 - SMOKE ALARMS USING SCATTERED LIGHT, TRANSMITTED LIGHT OR IONIZATION

HEALTH & AMENITY

- PART 10 OF THE NCC VOLUME 2, AMENDMENT 1 - BUILDING CODE OF AUSTRALIA 2022 & HOUSING PROVISIONS STANDARD 2022.
- AS/NZS ISO 717.1:2004 - ACOUSTICS - RATING OF SOUND INSULATION IN BUILDINGS & OF BUILDING ELEMENTS - AIRBORNE SOUND INSULATION
- AS ISO 717.2:2004 - ACOUSTICS - RATING OF SOUND INSULATION IN BUILDINGS & OF BUILDING ELEMENTS - IMPACT SOUND INSULATION
- AS 1668.2:2012 - THE USE OF VENTILATION & AIR CONDITIONING IN BUILDINGS - MECHANICAL VENTILATION IN BUILDINGS
- AS 1668.4:2012 - THE USE OF VENTILATION & AIR CONDITIONING IN BUILDINGS - NATURAL VENTILATION OF BUILDINGS
- AS/NZS 1680.0:2009 - INTERIOR LIGHTING - SAFE MOVEMENT
- AS 3740:2021 - WATERPROOFING OF DOMESTIC WET AREAS
- AS 3000:2018 – ELECTRICAL INSTALLATION
- BCA Part 10.8.1, AS4200.1 & AS4200.2 – PLIABLE BUILDING MEMBRANE INSTALLED.

WATERPROOFING

- PART 10.2 OF THE NCC VOLUME 2, AMENDMENT 1 - BUILDING CODE OF AUSTRALIA 2022 & HOUSING PROVISIONS STANDARD 2022
- AS 3740:2021– WATERPROOFING TO WET AREA
- AS 4654:2012 – EXTERNAL WET AREAS

SAFE MOVEMENT & ACCESS

- PART 11 OF THE NCC VOLUME 2, AMENDMENT 1 - BUILDING CODE OF AUSTRALIA 2022 & HOUSING PROVISIONS STANDARD 2022.
- AS 1428.1:2009 - DESIGN FOR ACCESS & MOBILITY – GENERAL REQUIREMENTS FOR ACCESS - NEW BUILDING WORK
- AS 1657:2018 - FIXED PLATFORMS, WALKWAYS, STAIRWAYS & LADDERS - DESIGN, CONSTRUCTION & INSTALLATION

Handrails & Balustrades Pty Ltd

- PART 11.3.9 OF THE NCC VOLUME 2, AMENDMENT 1 - BUILDING CODE OF AUSTRALIA 2022 & HOUSING PROVISIONS STANDARD 2022.
- PART 11.3.4 OF THE NCC VOLUME 2, AMENDMENT 1 - BUILDING CODE OF AUSTRALIA 2022 & HOUSING PROVISIONS STANDARD 2022.
- PART 11.3.5 OF THE NCC VOLUME 2, AMENDMENT 1 - BUILDING CODE OF AUSTRALIA 2022 & HOUSING PROVISIONS STANDARD 2022.
- AS 1170.1:2002 – BALUSTRADE INSTALLATION

PROTECTION OF OPENABLE WINDOW

PART 11.3.7 AND 11.3.8 OF THE NCC VOLUME 2, AMENDMENT 1 - BUILDING CODE OF AUSTRALIA 2022 & HOUSING PROVISIONS STANDARD 2022.

ENERGY EFFICIENCY

- PART 13 OF THE NCC VOLUME 2, AMENDMENT 1 - BUILDING CODE OF AUSTRALIA 2022 & HOUSING PROVISIONS STANDARD 2022 & BASIX CERTIFICATE.

MECHANICAL VENTILATION

- EXHAUST FROM A BATHROOM, SANITARY COMPARTMENT TO DISCHARGE DIRECTLY TO OUTDOOR AIR WITH MINIMUM FLOW RATE OF 25L/S & MAKE-UP AIR VIA OPENINGS TO AN ADJACENT ROOM WITH A FREE AREA OF 14,000 MM². THIS EXHAUST SYSTEM MUST BE INTERLOCKED WITH LIGHT SWITCH AND INCLUDE RUN-ON TIMER SO THAT THE EXHAUST SYSTEM CONTINUES TO OPERATE FOR 10 MINUTES AFTER THE LIGHT SWITCH IS OFF.
- ANY INSTALLED - KITCHEN RANGEHOOD EXHAUST TO DISCHARGE DIRECTLY OR VIA DUCT TO OUTDOOR AIR WITH MINIMUM FLOW RATE OF 40L/S & MAKE-UP AIR VIA OPENINGS TO AN ADJACENT ROOM WITH A FREE AREA OF 14,000 MM².
- LAUNDRY EXHAUST TO DISCHARGE DIRECTLY OR VIA DUCT TO OUTDOOR AIR WITH MINIMUM FLOW RATE OF 40L/S & MAKE-UP AIR VIA OPENINGS TO AN ADJACENT ROOM WITH A FREE AREA OF 14,000 MM².



REV	DATE	DESCRIPTION	BY
3	12-06-2026	Area increased	
2	10-06-2026	Building flipped as per WAE, 230 brick wall in Garage, Garage slope made 5 degrees	



THIS DRAWING IS THE EXCLUSIVE PROPERTY OF THE DEVELOPER & THE REPRODUCTION OF ANY PART WITHOUT THE PRIOR WRITTEN CONSENT OF THE DEVELOPER IS A VIOLATION OF APPLICABLE LAWS. IN NO EVENT SHALL THE DEVELOPER BE HELD LIABLE FOR SPECIAL, COLLATERAL, INCIDENTAL OR CONSEQUENTIAL LIABILITY IN CONNECTION WITH THE USE OF THIS DIGITAL DATA, ONCE RELEASED FROM THE DEVELOPER'S OFFICE. THIS DRAWING IS TO BE READ & UNDERSTOOD IN CONJUNCTION WITH THE STRUCTURAL, MECHANICAL, ELECTRICAL & / OR ANY OTHER CONSULTANTS' DOCUMENTATION AS MAY BE APPLICABLE TO THE PROJECT PRIOR TO THE START OF ANY WORKS AND FOR ITS DURATION.

PROJECT:
LOT 124

DRAWING TITLE:
GENERAL NOTES

45 MERIDIAN STREET,
LEPPINGTON

DRAWING No. **3**

DATE: **27-07-2026**

SCALE: **1 : 2**

DRAWN BY: **AS**

CHECKED BY: **RH**

DRAFTED BY: **ID**

CLIENT NAME: **Owner**

ISSUED BY: **CDC.02A**

CDC ISSUE

TERMITE SHEET

- TERMITE SHEET EXTENDS THROUGH THE ENTIRE MASONRY LEAF AND IS VISIBLE AT THE FINISHED FACE OF THE WALL.


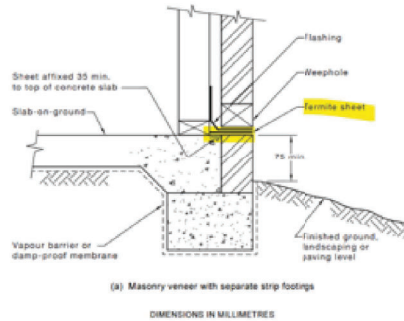


FIGURE 5.5 (in part) TYPICAL SHEET INSTALLATION TO EXTERNAL WALL WITH CONCRETE FLOOR SLAB

DPC FOR BRICKS

DAMP-PROOF COURSE (DPC) TO EXTENDS THROUGH THE ENTIRE MASONRY LEAF AND NEED TO BE VISIBLE AT THE FINISHED FACE OF THE WALL FROM OUTSIDE

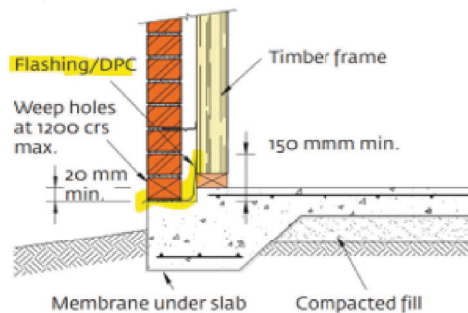

DEMOLITION

- AS 2601-2001 – DEMOLITION WORK

PLANTER BOX

REFER BELOW DETAILS FOR PLANTER BOX.



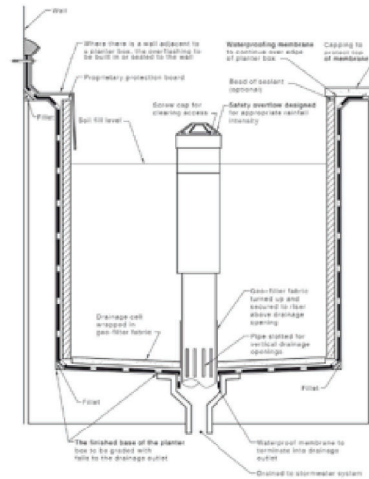


FIGURE 2.17 TYPICAL PLANTER BOX CONSTRUCTION

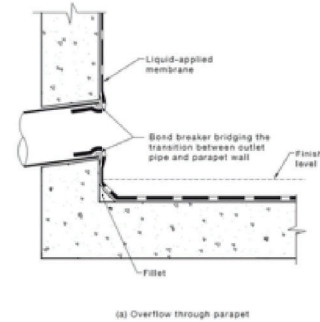

OVERFLOW TO BALCONY:

- SURFACE DRAIN & OVERFLOW TO BALCONY

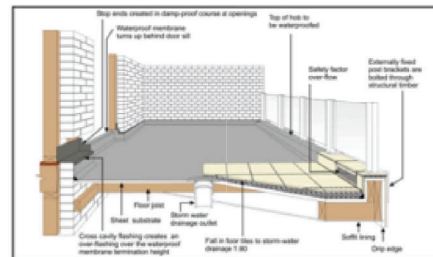

SWIMMING POOL

- PART 12.1.1 (H7D2) OF THE NCC VOLUME 2, AMENDMENT 1 - BUILDING CODE OF AUSTRALIA 2022 & HOUSING PROVISIONS STANDARD 2022
- AS 1926 PART 1-2012 – SWIMMING POOLSAFETY- SAFETY BARRIERS FOR SWIMMING POOLS
- AS 1926 PART 2-2007 - SWIMMING POOL SAFETY- LOCATION OF SAFETY BARRIERS FOR SWIMMING POOLS (INCORPORATING AMENDMENTS 1 AND 2)
- AS 1926 PART 3-2010 – SWIMMING POOL SAFETY- WATER RECIRCULATION SYSTEMS (INCORPORATING AMENDMENT 1)

OnBuild Certifiers Pty Ltd

Reference: 260043

Date: 03/08/2026

Andrew Soliman

Director/ Principal Certifier

BDC2940

Consultant who prepared this document remains responsible for accuracy

REV	DATE	DESCRIPTION	BY
3	12-06-2026	Area increased	
2	10-06-2026	Building flipped as per WAE, 230 brick wall in Garage, Garage slope made 5 degrees	



THIS DRAWING IS THE EXCLUSIVE PROPERTY OF THE DEVELOPER & THE REPRODUCTION OF ANY PART WITHOUT THE PRIOR WRITTEN CONSENT OF THE DEVELOPER IS A VIOLATION OF APPLICABLE LAWS. IN NO EVENT SHALL THE DEVELOPER BE HELD LIABLE FOR SPECIAL, COLLATERAL, INCIDENTAL OR CONSEQUENTIAL LIABILITY IN CONNECTION WITH THE USE OF THIS DIGITAL DATA, ONCE RELEASED FROM THE DEVELOPER'S OFFICE. THIS DRAWING IS TO BE READ & UNDERSTOOD IN CONJUNCTION WITH THE STRUCTURAL, MECHANICAL, ELECTRICAL & FOR ANY OTHER CONSULTANTS' DOCUMENTATION AS MAY BE APPLICABLE TO THE PROJECT PRIOR TO THE START OF ANY WORKS AND FOR ITS DURATION.

PROJECT:
LOT 124

45 MERIDIAN STREET,
LEPPINGTON

DRAWING TITLE:
GENERAL NOTES

NORTH:


LOT NO:	DATE:	SCALE:	DRAWING No.	REV:
124	27-07-2026	1 : 2	CDC.02B	3
DRAWN BY:	CHECKED BY:	DRAFTED BY:	CLIENT NAME:	ISSUED BY:
AS	RH	ID	Owner	

DETAILS SHOWN ON THE PLANS ARE INTENDED TO BE ACCURATE. HOWEVER, BUILDER/SUPERVISOR RESERVE THE RIGHT TO ADJUST THE MEASUREMENT/ITEMS AS REQUIRED DUE TO SITE CONDITIONS.

Reference: 260043


Date: 03/08/2026

AREA SCHEDULE	
Director/ Principal Certifier	AREA (m2)
LOT AREA	300.1
GROUND FLOOR	102
FIRST FLOOR	103
GARAGE	33
STAIRCASE VOID	13
PRIVATE OPEN SPACE	24
DRIVEWAY	29
FRONT LANDSCAPE	31.7
REAR LANDSCAPE	38.3

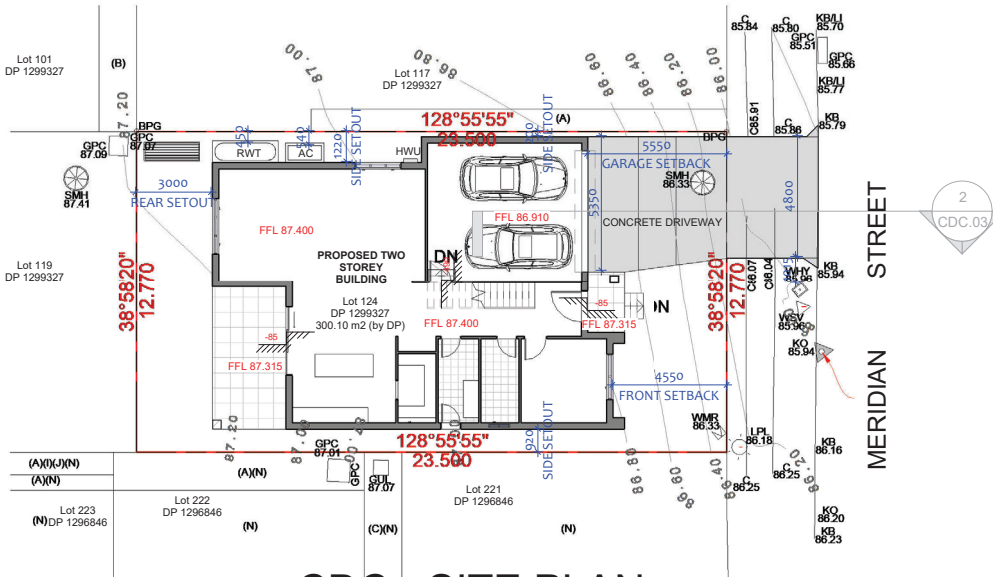

CDC - SITE PLAN

1
1 : 200

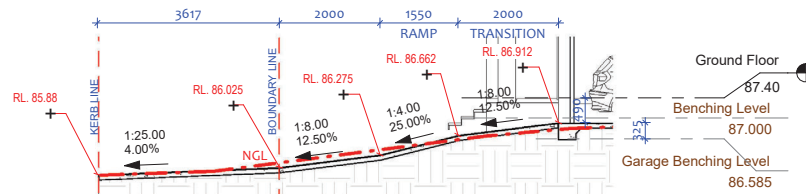

DRIVEWAY SECTION

2
1 : 100

- (A) EASEMENT FOR SUPPORT AND MAINTENANCE 0.9 WIDE (DP 1299327)
(B) EASEMENT FOR DRAINAGE OF WATER 1.5 WIDE
(A) EASEMENT TO DRAIN WATER 1.5 WIDE (DP 1296846)
(I) POSITIVE COVENANT 0.9 WIDE (SITE)(NO.6)
(J) RESTRICTION ON THE USE OF LAND 0.9 WIDE (SITE)(NO.7)
(N) RESTRICTION ON THE USE OF LAND (NO.13) (SITE)

GREENFIELD HOUSING CODE COMPLIANCE TABLE

DESCRIPTION		COMPLIANCE		COMMENT
ELEMENT	CODE CONTROL	REQUIREMENT	PROPOSED	
LAND ZONE	R2 LOW DENSITY RESIDENTIAL			
LOT NO	LOT 124			
LOT AREA	300.10 m2			
LOT WIDTH	Standard Lot Min. 6m at Building Line facing primary road	6.0m	12.77 m	YES
HEIGHT	MAX. Height	8.5m	8.0m (MAX.)	YES
FRONT SETBACK	FRONT SET BACK (Min. Setback from Primary Road) For 300-350 sqm. Lot	4.5 m	4.55m	YES
REAR SET BACK (MIN.)	GROUND FLOOR	3m	3m	YES
	FIRST FLOOR	6m	6 m	
SIDE SET BACK (MIN.)	GROUND FLOOR	0/0.9m	0.2/0.92m	YES
	FIRST FLOOR	1.2/0.9m	1.2/0.92m	
GROSS FLOOR AREA (GFA)	235m2	235m2	226 m2	YES
GROSS FLOOR AREA PLAN	GROUND FLOOR		105 m2	
	FIRST FLOOR		106 m2	
GARAGE			33m2	
TOTAL FLOOR AREA			226 m2	
ROOF AREA			207m2	
PRIVATE OPEN SPACE	>10m Lot width	24m2	24 m2	YES
LANDSCAPE AREA	15 % of TOTAL LAND AREA	45.015 m2	70 m2	YES

CDC ISSUE

REV	DATE	DESCRIPTION	BY
3	12-06-2026	Area increased	
2	10-06-2026	Building flipped as per WAE, 230 brick wall in Garage, Garage slope made 5 degrees	



THIS DRAWING IS THE EXCLUSIVE PROPERTY OF THE DEVELOPER & THE REPRODUCTION OF ANY PART WITHOUT THE PRIOR WRITTEN CONSENT OF THE DEVELOPER IS A VIOLATION OF APPLICABLE LAWS. IN NO EVENT SHALL THE DEVELOPER BE HELD LIABLE FOR SPECIAL, COLLATERAL, INCIDENTAL OR CONSEQUENTIAL LIABILITY IN CONNECTION WITH THE USE OF THIS DIGITAL DATA, ONCE RELEASED FROM THE DEVELOPER'S OFFICE. THIS DRAWING IS TO BE READ & UNDERSTOOD IN CONJUNCTION WITH THE STRUCTURAL, MECHANICAL, ELECTRICAL & / OR ANY OTHER CONSULTANTS' DOCUMENTATION AS MAY BE APPLICABLE TO THE PROJECT PRIOR TO THE START OF ANY WORKS AND FOR ITS DURATION.

PROJECT:
LOT 124


45 MERIDIAN STREET,
LEPPINGTON

DRAWING TITLE:
LOCATION PLAN
AND SITE PLAN

NORTH:







LOT NO: 124	DATE: 27-07-2026	SCALE: As indicated	DRAWING No. CDC.03	REV: 3
DRAWN BY: AS	CHECKED BY: RH			
DRAFTED BY: ID	CLIENT NAME: Owner			

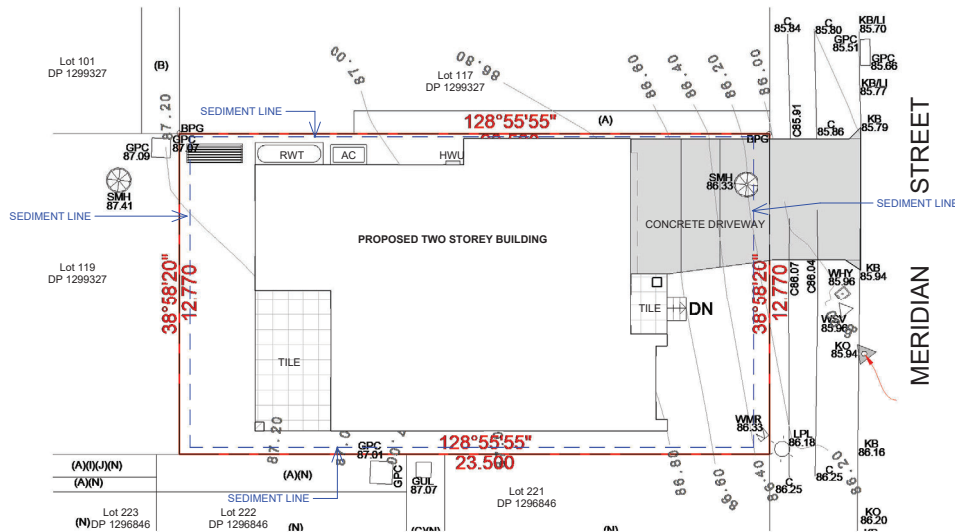

1
CDC - SITE ANALYSIS AND SEDIMENT CONTROL
1 : 200

SD 5-7 STABILISED SITE ACCESS

- 1) STRIP TOPSOIL AND LEVEL SITE.
- 2) COMPACT SUBGRADE.
- 3) COVER AREA WITH GEOTEXILE.
- 4) CONSTRUCT 200 mm THICK PAD OVER GEOTEXILE USING ROADBASE OR 30 mm AGGREGATE. Min 15 m LONG OR TO BUILDING ALIGNMENT. Min 3 m WIDE.
- 5) CONSTRUCT HUMP IMMEDIATELY WITHIN BOUNDARY TO DIVERT WATER TO A SEDIMENT FENCE OR OTHER SEDIMENT TRAP.

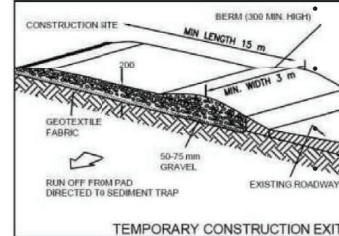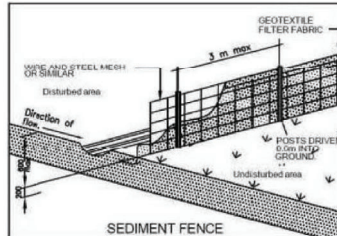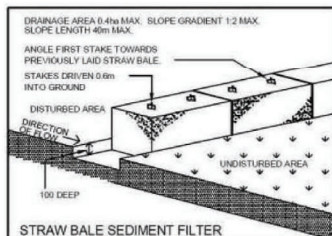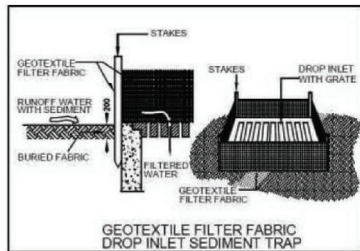

TEMPORARY 1.8M HIGH WIRE MESH FENCE WITH DUSTPROOF MESH APPLIED TO FULL HEIGHT TO BOUNDARIES AS REQUIRED

LOCATION OF WASTE BINS

SEDIMENT FENCE AS REQUIRED

GRAVEL ACCESS

SITE ACCESS AREA TO BE USED FOR WASHDOWN AREA

FOOTPATH CLEAN AND CLEAR AT ALL TIMES

LOCATION OF STOCKPILE MATERIAL

MATERIAL STORAGE AREA

TEMPORARY TOILETS

INSTALL TEMPORARY SEDIMENT BARRIERS TO ALL INLET PITS LIKELY TO COLLECT SILT LADEN WATER, TO COUNCIL'S REQUIREMENTS.

SD 6-9 GEOTEXTILE INLET FILTER

- 1) FABRICATE A SEDIMENT BARRIER MADE FROM GEOTEXILE. REFER SD6-7 FOR DETAILS.
- 2) SUPPORT GEOTEXILE WITH MESH TIED TO POSTS AT 1 m Ctrs.
- 3) DO NOT COVER INLET WITH GEOTEXILE.

SITE WORKS NOTES

1. ORIGIN OF LEVELS PROVIDED BY SURVEYOR
2. THE BUILDER SHALL VERIFY ALL DIMENSIONS AND EXISTING LEVELS ON SITE PRIOR TO THE COMMENCEMENT OF WORK AND ANY DISCREPANCIES SHALL BE REPORTED TO THE SURVEYOR / ENGINEER.
3. TOPSOIL SHALL BE STRIPPED FROM THE CONSTRUCTION AREA AND STOCKPILED ON SITE, TO BE LATER SPREAD OR DISPOSED OFF SITE, AS DIRECTED BY SUPERVISOR / ENGINEER.
4. ALL TRENCH BACKFILL MATERIAL SHALL BE COMPACTED TO THE SAME DENSITY AS THE ADJACENT MATERIAL.
5. ALL SERVICE TRENCHES UNDER VEHICULAR PAVEMENTS SHALL BE BACKFILLED WITH SAND OR APPROVED GRANULAR MATERIALS, TO THE UNDERSIDE OF THE PAVEMENT, AND COMPACTED TO 98% STANDARD MAXIMUM DRY DENSITY, IN ACCORDANCE WITH AS 1289E1.1.

SEDIMENT AND EROSION NOTES:

- THIS PLAN TO BE READ IN CONJUNCTION WITH SEDIMENT AND EROSION CONTROL DETAILS AS ATTACHED.
- THE CONTRACTOR SHALL IMPLEMENT ALL SOIL EROSION AND SEDIMENT CONTROL MEASURES AS NECESSARY AND TO THE SATISFACTION OF COUNCIL PRIOR TO THE COMMENCEMENT AND DURING CONSTRUCTION. NO DISTURBANCE TO THE SITE SHALL BE PERMITTED OTHER THAN IN THE IMMEDIATE AREA OF THE WORK AND NO MATERIAL SHALL BE REMOVED FROM THE SITE WITHOUT COUNCIL'S APPROVAL. ALL SEDIMENT AND EROSION CONTROL DEVICES TO BE INSTALLED AND MAINTAINED IN ACCORDANCE WITH STANDARDS OUTLINED IN NSW DEPARTMENT OF HOUSING "MANAGING URBAN STORMWATER-SOILS AND CONSTRUCTIONS".
- TOPSOIL SHALL BE STRIPPED AND STOCKPILED OUTSIDE HAZARD AREAS SUCH AS DRAINAGE LINES. THIS TOP SOIL IS TO BE RESPIRED LATER ON AREAS TO BE REVEGETATED AND STABILISED ONLY. (I.E ALL FOOTPATHS, BATTERS, SITE REGARDING AREAS, BASINS AND CATCH DRAINS), TOPSOIL SHALL NOT BE RESPIRED ON ANY OTHER AREAS UNLESS SPECIALLY INSTRUCTED BY THE SUPERINTENDENT. IF THEY ARE TO REMAIN FOR LONGER THAN ONE MONTH STOCKPILES SHALL BE PROTECTED FROM EROSION BY COVERING THEM WITH A MULCH AND HYDROSEEDING AND, IF NECESSARY, BY LOCATING BANKS OR DRAINS DOWNSTREAM OF A STOCKPILE TO RETARD SILT LADEN RUNOFF.
- THE CONTRACTOR SHALL REGULARLY MAINTAIN ALL SEDIMENT AND EROSION CONTROL DEVICES AND REMOVE ACCUMULATED SILT FROM SUCH DEVICES SUCH THAT MORE THAN 60% OF THEIR CAPACITY LOST. ALL THE SILTS TO BE PLACED OUTSIDE THE LIMIT OF WORKS. THE PERIOD FOR MAINTAINING THESE DEVICES SHALL BE AT LEAST UNTIL ALL DISTURBED AREAS ARE REVEGETATED AND FURTHER AS MAY BE DIRECTED BY THE SUPERINTENDENT OR COUNCIL.
- LAY TURF STRIP (MIN 300 mm WIDE) ON 100 mm TOPSOIL WITH 1.0 m LONG RETURNS EVERY 6.0m BEHIND ALL KERB AT THE TOP OF ALL BATTERS AND AROUND STRUCTURES IMMEDIATELY AFTER BACKFILLING OR FORMATION.
- THE CONTRACTOR SHALL GRASS SEED ALL DISTURBED AREAS WITH AN APPROVED MIX AS SS ON AS PRACTICABLE AFTER COMPLETION OF EARTHWORKS AND REGRADING.
- VEHICULAR TRAFFIC SHALL BE CONTROLLED DURING CONSTRUCTION CONFINING ACCESS WHERE POSSIBLE TO NOMINATED STABILISED ACCESS POINTS.
- WHEN ANY DEVICES ARE TO BE HANDED OVER TO COUNCIL, THEY SHALL BE IN CLEAN AND STABLE CONDITION.
- THE CONTRACTOR SHALL IMPLEMENT DUST CONTROL BY REGULAR WETTING DOWN (BUT NOT SATURATING) DISTURBED AREA.
- PROVIDE AND MAINTAIN SILT TRAPS AROUND ALL SURFACE INLET PITS UNTIL CATCHMENT IS REVEGETATED OR PAVED.
- REVEGETATE ALL TRENCHES IMMEDIATELY UPON COMPLETION OF BACKFILLING.
- ALL DRAINAGE PIPE INLETS TO BE CAPPED UNTIL:
 - A) DOWNPIPES CONNECTED
 - B) PITS CONSTRUCTED & PROTECTED WITH SILT BARRIER

REV	DATE	DESCRIPTION	BY
3	12-06-2026	Area increased	
2	10-06-2026	Building flipped as per WAE, 230 brick wall in Garage, Garage slope made 5 degrees	

NANDI CONSTRUCTIONS

THIS DRAWING IS THE EXCLUSIVE PROPERTY OF THE DEVELOPER & THE REPRODUCTION OF ANY PART WITHOUT THE PRIOR WRITTEN CONSENT OF THE DEVELOPER IS A VIOLATION OF APPLICABLE LAWS. IN NO EVENT SHALL THE DEVELOPER BE HELD LIABLE FOR SPECIAL, COLLATERAL, INCIDENTAL OR CONSEQUENTIAL LIABILITY IN CONNECTION WITH THE USE OF THIS DIGITAL DATA ONCE RELEASED FROM THE DEVELOPER'S OFFICE. THIS DRAWING IS TO BE READ & UNDERSTOOD IN CONJUNCTION WITH THE STRUCTURAL, MECHANICAL, ELECTRICAL & / OR ANY OTHER CONSULTANTS' DOCUMENTATION AS MAY BE APPLICABLE TO THE PROJECT PRIOR TO THE START OF ANY WORKS AND FOR ITS DURATION.

PROJECT:
LOT 124

45 MERIDIAN STREET,
LEPPINGTON


DRAWING TITLE:
**SITE ANALYSIS
AND SEDIMENT
CONTROL**

NORTH:

LOT NO:	DATE:	SCALE:	DRAWING No.	REV:
124	27-07-2026	As indicated	CDC.04	3
DRAWN BY:	CHECKED BY:	CLIENT NAME:	ISSUED BY:	
AS	RH	Owner		
DRAFTED BY:	ID			

OnBuild Construction Ltd
Reference: **124**
Date: **27-07-2026**
Andrew Solomon
Director/Principal Designer
BPC 3540
Consultant who prepared this document remains responsible

IMPORTANT NOTES:
 ALL DIMENSIONS AND NOTES ON ALL PLANS MUST BE CHECKED AND VERIFIED BY BUILDERS AND OWNER PRIOR TO COMMENCEMENT OF ANY BUILDING WORKS. TO CLARIFY AND CONFIRM WITH CONSTRUCTION COMPANY FOR DISCREPANCIES ON ALL DOCUMENTS AND PLANS PROVIDED FOR CONSTRUCTION ANY WORK INDICATED ON THE PLAN BUT NOT IN CONTRACT VARIATION TO PLANS SPECIFICATIONS MAY NOT BE RESPONSIBILITY OF THE BUILDER END USER TO VERIFY PLANS CURRENT BCA AND AUSTRALIAN STANDARDS. WINDOWS TO COMPLY WITH 3.9.3.5 OF THE BCA. DETAILS SHOWN ON THE PLANS ARE INTENDED TO BE ACCURATE. HOWEVER, BUILDER SUPERVISOR RESERVE THE RIGHT TO ADJUST THE MEASUREMENTS AS REQUIRED DUE TO SITE CONDITIONS.

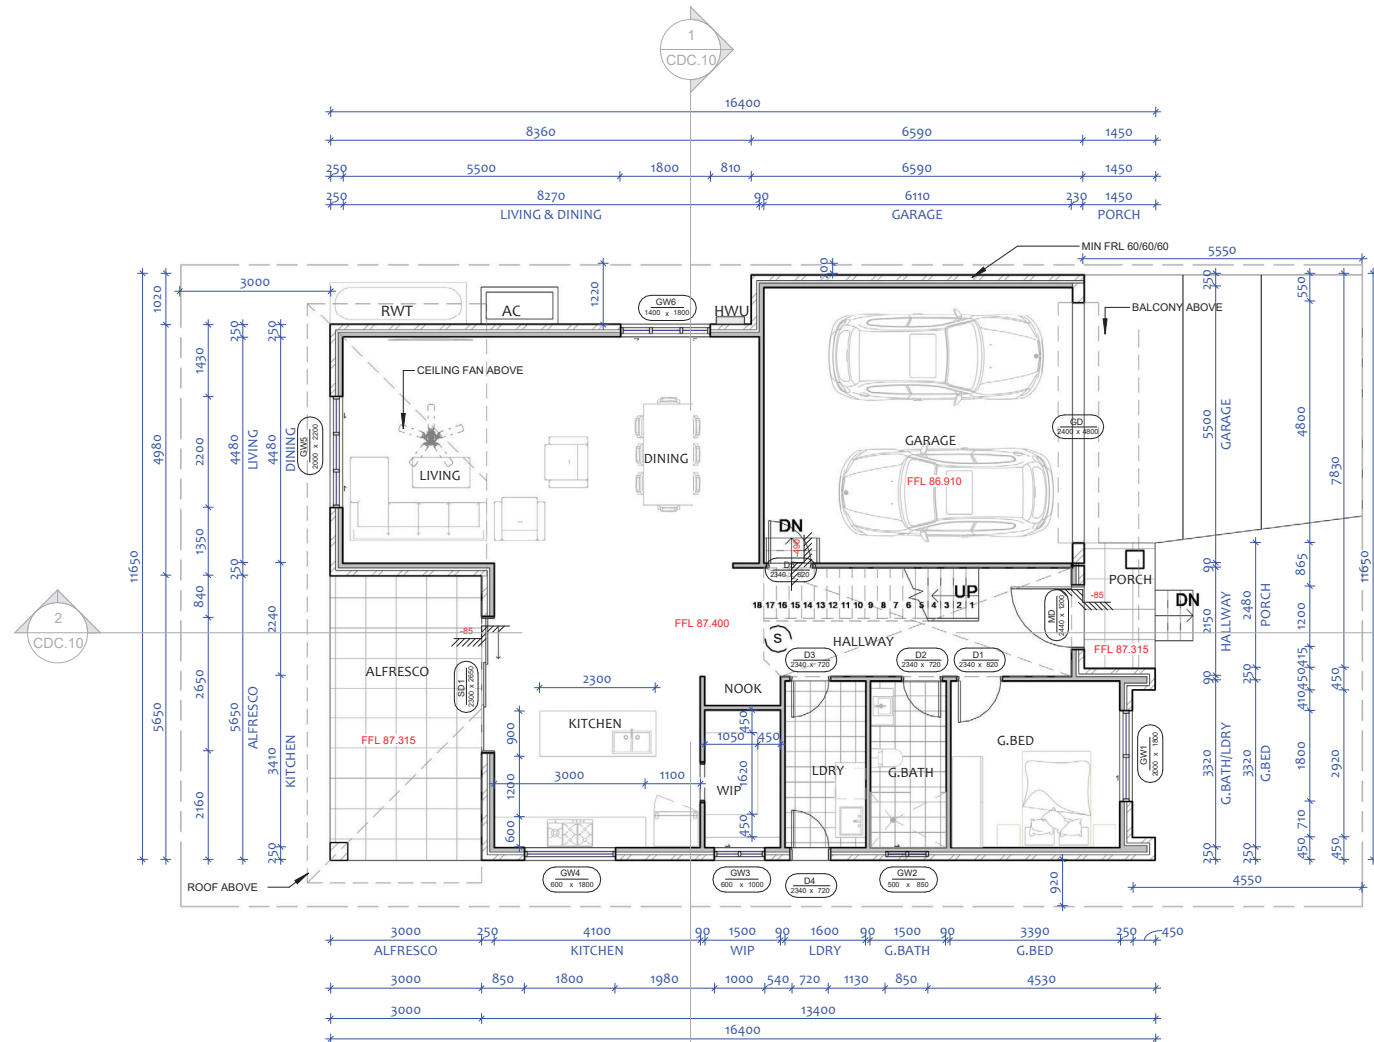

1 **Ground Floor**
 1 : 100

NOTE: PLEASE REFER TO TENDER FOR ALL INCLUSIONS.


REV	DATE	DESCRIPTION	BY
3	12-06-2026	Area increased	
2	10-06-2026	Building flipped as per WAE, 230 brick wall in Garage, Garage slope made 5 degrees	
1	13-03-2026	Bank Set	



THIS DRAWING IS THE EXCLUSIVE PROPERTY OF THE DEVELOPER & THE REPRODUCTION OF ANY PART WITHOUT THE PRIOR WRITTEN CONSENT OF THE DEVELOPER IS A VIOLATION OF APPLICABLE LAWS. IN NO EVENT SHALL THE DEVELOPER BE HELD LIABLE FOR SPECIAL, COLLATERAL, INCIDENTAL OR CONSEQUENTIAL LIABILITY IN CONNECTION WITH THE USE OF THIS DIGITAL DATA, ONCE RELEASED FROM THE DEVELOPER'S OFFICE. THIS DRAWING IS TO BE READ & UNDERSTOOD IN CONJUNCTION WITH THE STRUCTURAL, MECHANICAL, ELECTRICAL & / OR ANY OTHER CONSULTANTS' DOCUMENTATION AS MAY BE APPLICABLE TO THE PROJECT PRIOR TO THE START OF ANY WORKS AND FOR ITS DURATION.

PROJECT:
LOT 124
 45 MERIDIAN STREET,
 LEPPINGTON


DRAWING TITLE:
**GROUND FLOOR
 PLAN**

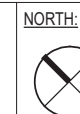

LOT NO:	DATE:	SCALE:	DRAWING No.	REV:
124	27-07-2026	1 : 100	CDC.05	3
DRAWN BY:	CHECKED BY:	DRAFTED BY:	CLIENT NAME:	ISSUED BY:
AS	RH	ID	Owner	

OnBuild Construction Ltd
Referenced by
Date: 27-07-2026
Andrew Seaman
Director/ Principal Designer
BACS TEAM
Consultant who prepared this document remains responsible

IMPORTANT NOTES:
ALL DIMENSIONS AND NOTES ON ALL PLANS MUST BE CHECKED AND VERIFIED BY BUILDERS AND OWNER PRIOR TO COMMENCEMENT OF ANY BUILDING WORKS. TO CLARIFY AND CONFIRM WITH CONSTRUCTION COMPANY FOR DISCREPANCIES ON ALL DOCUMENTS AND PLANS PROVIDED FOR CONSTRUCTION. ANY WORK INDICATED ON THE PLAN BUT NOT IN CONTRACT, VARIATION TO PLANS SPECIFICATIONS MAY NOT BE THE RESPONSIBILITY OF THE BUILDER. END USER TO VERIFY PLANS CURRENT BCA AND AUSTRALIAN STANDARDS. WINDOWS TO COMPLY WITH 3.9.3.5 OF THE BCA. DETAILS SHOWN ON THE PLANS ARE INTENDED TO BE ACCURATE. HOWEVER, BUILDER SUPERVISOR RESERVE THE RIGHT TO ADJUST THE MEASUREMENTS AS REQUIRED DUE TO SITE CONDITIONS.

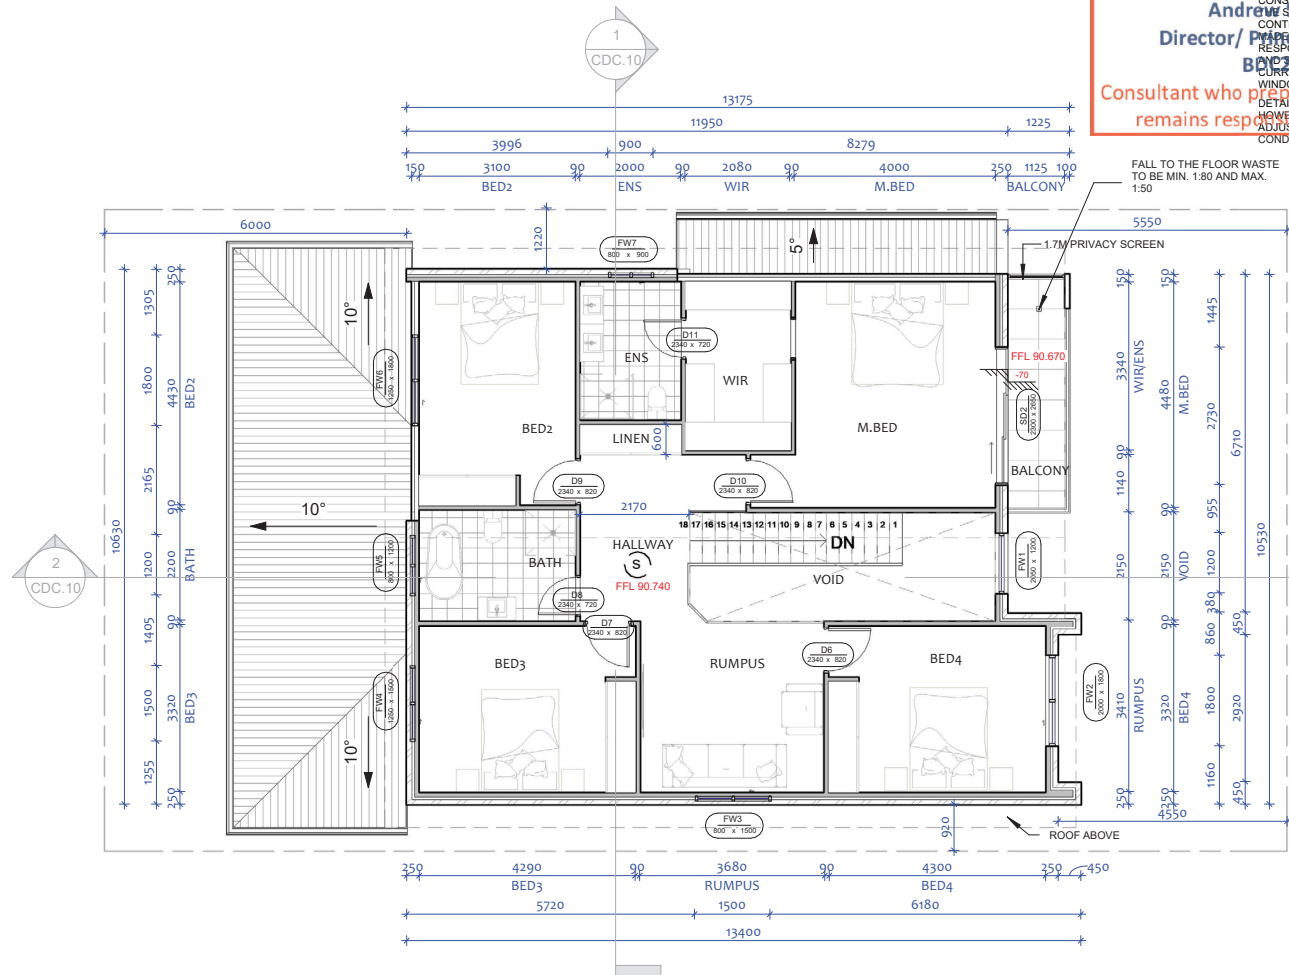

1 Level 1
1 : 100

NOTE: PLEASE REFER TO TENDER FOR ALL INCLUSIONS.

REV	DATE	DESCRIPTION	BY
3	12-06-2026	Area increased	
2	10-06-2026	Building flipped as per WAE, 230 brick wall in Garage, Garage slope made 5 degrees	
1	13-03-2026	Bank Set	

NANDI CONSTRUCTIONS

THIS DRAWING IS THE EXCLUSIVE PROPERTY OF THE DEVELOPER & THE REPRODUCTION OF ANY PART WITHOUT THE PRIOR WRITTEN CONSENT OF THE DEVELOPER IS A VIOLATION OF APPLICABLE LAWS. IN NO EVENT SHALL THE DEVELOPER BE HELD LIABLE FOR SPECIAL, COLLATERAL, INCIDENTAL OR CONSEQUENTIAL LIABILITY IN CONNECTION WITH THE USE OF THIS DIGITAL DATA, ONCE RELEASED FROM THE DEVELOPER'S OFFICE. THIS DRAWING IS TO BE READ & UNDERSTOOD IN CONJUNCTION WITH THE STRUCTURAL, MECHANICAL, ELECTRICAL & / OR ANY OTHER CONSULTANTS' DOCUMENTATION AS MAY BE APPLICABLE TO THE PROJECT PRIOR TO THE START OF ANY WORKS AND FOR ITS DURATION.

PROJECT:
LOT 124

45 MERIDIAN STREET,
LEPPINGTON


DRAWING TITLE:
FIRST FLOOR LEVEL

NORTH:

LOT NO:	DATE:	SCALE:	DRAWING No.	REV:
124	27-07-2026	1 : 100	CDC.06	3
DRAWN BY:	CHECKED BY:	CLIENT NAME:	ISSUED BY:	
AS	RH	Owner		
DRAFTED BY:				
ID				

OnBuild Construction Ltd
Referenced by:
Date: 27-07-2026
Andrew Seaman
Director/ Principal Designer
BPC 3541
Consultant who prepared this document remains responsible

IMPORTANT NOTES:
ALL DIMENSIONS AND NOTES ON ALL PLANS MUST BE CHECKED AND VERIFIED BY BUILDERS AND OWNER PRIOR TO COMMENCEMENT OF ANY BUILDING WORKS, TO CLARIFY AND CONFIRM WITH CONSTRUCTION COMPANY FOR DISCREPANCIES ON ALL DOCUMENTS AND PLANS PROVIDED FOR CONSTRUCTION. ANY WORK INDICATED ON THE PLAN BUT NOT IN CONTRACT, VARIATION TO PLANS, SPECIFICATIONS MAY NOT BE THE RESPONSIBILITY OF THE BUILDING END USER TO VERIFY PLANS CURRENT BCA AND AUSTRALIAN STANDARDS. WINDOWS TO COMPLY WITH 3.9.3.5 OF THE BCA. DETAILS SHOWN ON THE PLANS ARE INTENDED TO BE ACCURATE. HOWEVER, BUILDER SUPERVISOR RESERVE THE RIGHT TO ADJUST THE MEASUREMENTS AS REQUIRED DUE TO SITE CONDITIONS.

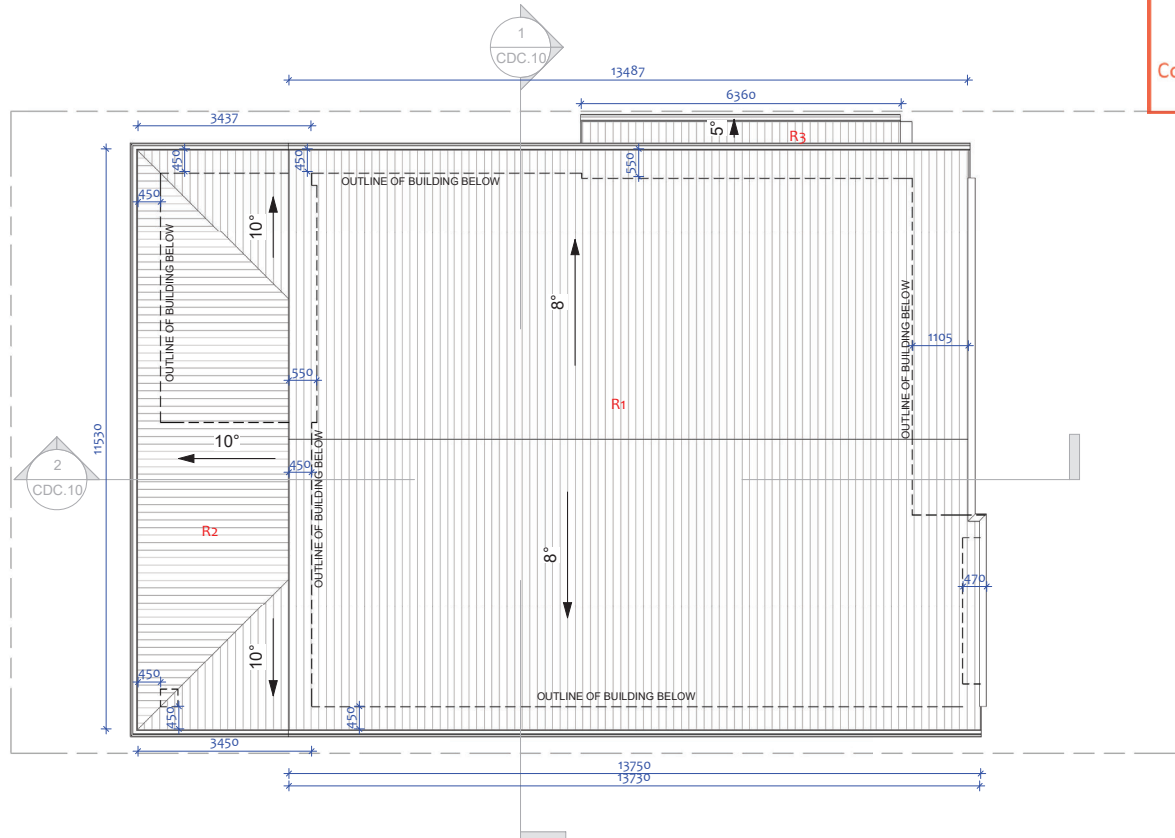

1 ROOF PLAN
1 : 100

Roof Schedule			
Mark	Base Level	Area	Comments
R3	Level 1	7 m ²	COLORBOND
R2	Level 1	41 m ²	COLORBOND
R1	CEILING LEVEL	158 m ²	COLORBOND
Grand total: 3		207 m ²	

REV	DATE	DESCRIPTION	BY
3	12-06-2026	Area increased	
2	10-06-2026	Building flipped as per WAE, 230 brick wall in Garage, Garage slope made 5 degrees	
1	13-03-2026	Bank Set	


NANDI CONSTRUCTIONS

THIS DRAWING IS THE EXCLUSIVE PROPERTY OF THE DEVELOPER & THE REPRODUCTION OF ANY PART WITHOUT THE PRIOR WRITTEN CONSENT OF THE DEVELOPER IS A VIOLATION OF APPLICABLE LAWS. IN NO EVENT SHALL THE DEVELOPER BE HELD LIABLE FOR SPECIAL, COLLATERAL, INCIDENTAL OR CONSEQUENTIAL LIABILITY IN CONNECTION WITH THE USE OF THIS DIGITAL DATA, ONCE RELEASED FROM THE DEVELOPER'S OFFICE. THIS DRAWING IS TO BE READ & UNDERSTOOD IN CONJUNCTION WITH THE STRUCTURAL, MECHANICAL, ELECTRICAL & / OR ANY OTHER CONSULTANTS' DOCUMENTATION AS MAY BE APPLICABLE TO THE PROJECT PRIOR TO THE START OF ANY WORKS AND FOR ITS DURATION.


PROJECT:
LOT 124

45 MERIDIAN STREET,
LEPPINGTON

DRAWING TITLE:
ROOF PLAN

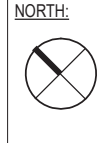


LOT NO:	DATE:	SCALE:	DRAWING No.	REV:
124	27-07-2026	1 : 100	CDC.07	3
DRAWN BY:	CHECKED BY:	DRAFTED BY:	CLIENT NAME:	ISSUED BY:
AS	RH	ID	Owner	

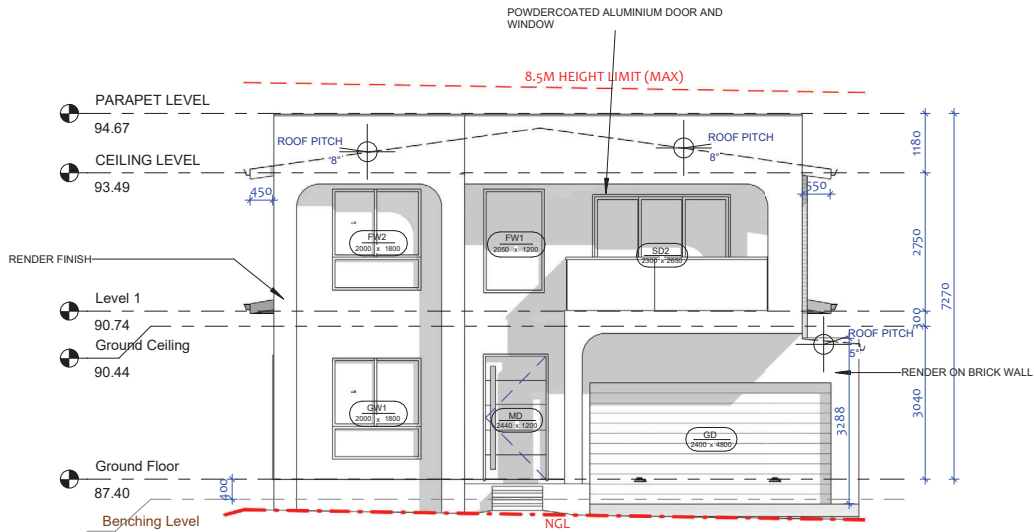

SOUTH-EAST ELEVATION

1 : 100

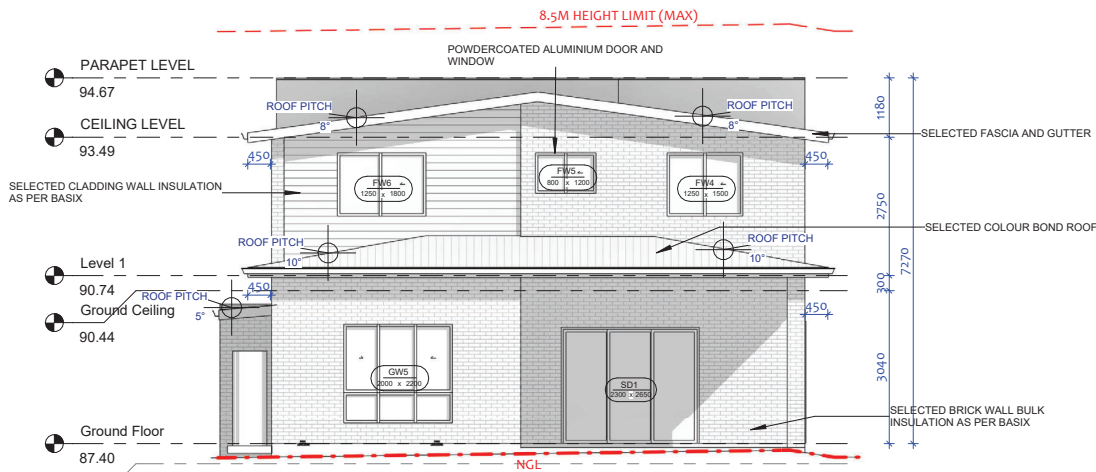

NORTH-WEST ELEVATION

1 : 100

DETAILS SHOWN ON THE PLANS ARE INTENDED TO BE ACCURATE. HOWEVER, BUILDER/SUPERVISOR RESERVE THE RIGHT TO ADJUST THE MEASUREMENT/ITEMS AS REQUIRED DUE TO SITE CONDITIONS.

Reference: 260043

Date: 03/08/2026

Andrew Soliman

Director / Principal Certifier

BDC2940

Consultant who prepared this document remains responsible for accuracy

Mark	Height	Width	Sill Height	Head Height	Description
------	--------	-------	-------------	-------------	-------------

Ground Floor

GW1	2000	1800	400	2400	SLIDING
GW2	500	850	1900	2400	SLIDING
GW3	600	1000	1050	1650	SLIDING
GW4	600	1800	1050	1650	FIXED
GW5	2000	2200	400	2400	SLIDING & FIXED
GW6	1400	1800	1000	2400	SLIDING

Ground Floor: 6

Level 1

FW1	2050	1200	400	2450	FIXED
FW2	2000	1800	450	2450	SLIDING
FW3	800	1500	1650	2450	SLIDING
FW4	1250	1500	1200	2450	SLIDING
FW5	800	1200	1650	2450	SLIDING
FW6	1250	1800	1200	2450	SLIDING
FW7	800	900	1650	2450	SLIDING

Level 1: 7

Door Schedule 1

Mark	Height	Width	Count	Description
------	--------	-------	-------	-------------

Ground Floor

D1	2340	820	1	FLUSH DOOR
D2	2340	720	1	FLUSH DOOR
D3	2340	720	1	FLUSH DOOR
D4	2340	720	1	FLUSH DOOR
D5	2340	820	1	FLUSH DOOR
GD	2400	4800	1	GARAGE DOOR
MD	2440	1200	1	SOLID CORE DOOR
SD1	2300	2650	1	SLIDING DOOR

Ground Floor: 8

Level 1

D6	2340	820	1	FLUSH DOOR
D7	2340	820	1	FLUSH DOOR
D8	2340	720	1	FLUSH DOOR
D9	2340	820	1	FLUSH DOOR
D10	2340	820	1	FLUSH DOOR
D11	2340	720	1	FLUSH DOOR
SD2	2300	2650	1	SLIDING DOOR

Level 1: 7

CDC ISSUE

REV	DATE	DESCRIPTION	BY
3	12-06-2026	Area increased	
2	10-06-2026	Building flipped as per WAE, 230 brick wall in Garage, Garage slope made 5 degrees	
1	13-03-2026	Bank Set	



THIS DRAWING IS THE EXCLUSIVE PROPERTY OF THE DEVELOPER & THE REPRODUCTION OF ANY PART WITHOUT THE PRIOR WRITTEN CONSENT OF THE DEVELOPER IS A VIOLATION OF APPLICABLE LAWS. IN NO EVENT SHALL THE DEVELOPER BE HELD LIABLE FOR SPECIAL, COLLATERAL, INCIDENTAL OR CONSEQUENTIAL LIABILITY IN CONNECTION WITH THE USE OF THIS DIGITAL DATA, ONCE RELEASED FROM THE DEVELOPER'S OFFICE. THIS DRAWING IS TO BE READ & UNDERSTOOD IN CONJUNCTION WITH THE STRUCTURAL, MECHANICAL, ELECTRICAL & / OR ANY OTHER CONSULTANTS' DOCUMENTATION AS MAY BE APPLICABLE TO THE PROJECT PRIOR TO THE START OF ANY WORKS AND FOR ITS DURATION.

PROJECT:
LOT 124

45 MERIDIAN STREET,
LEPPINGTON

DRAWING TITLE:
ELEVATION 01

NORTH:

LOT NO: 124	DATE: 27-07-2026	SCALE: 1 : 100	DRAWING No. CDC.08	REV: 3
DRAWN BY: AS	CHECKED BY: RH	CLIENT NAME: Owner	ISSUED BY:	
DRAFTED BY: ID				

DETAILS SHOWN ON THE PLANS ARE INTENDED TO BE ACCURATE. HOWEVER, BUILDERS SUPERVISOR RESERVE THE RIGHT TO ADJUST THE MEASUREMENT/ITEMS AS REQUIRED DUE TO SITE CONDITIONS.

Reference: 260043


Date: 03/08/2026

Andrew Soliman


Director/ Principal Certifier

BDC2940

Consultant who prepared this document
remains responsible for accuracy

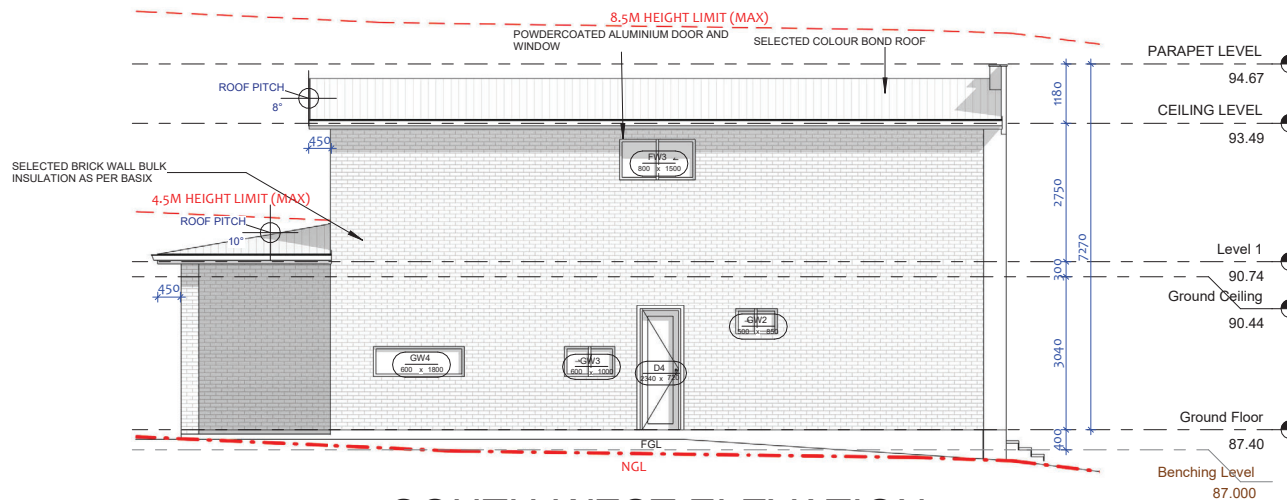

1 SOUTH-WEST ELEVATION
1 : 100

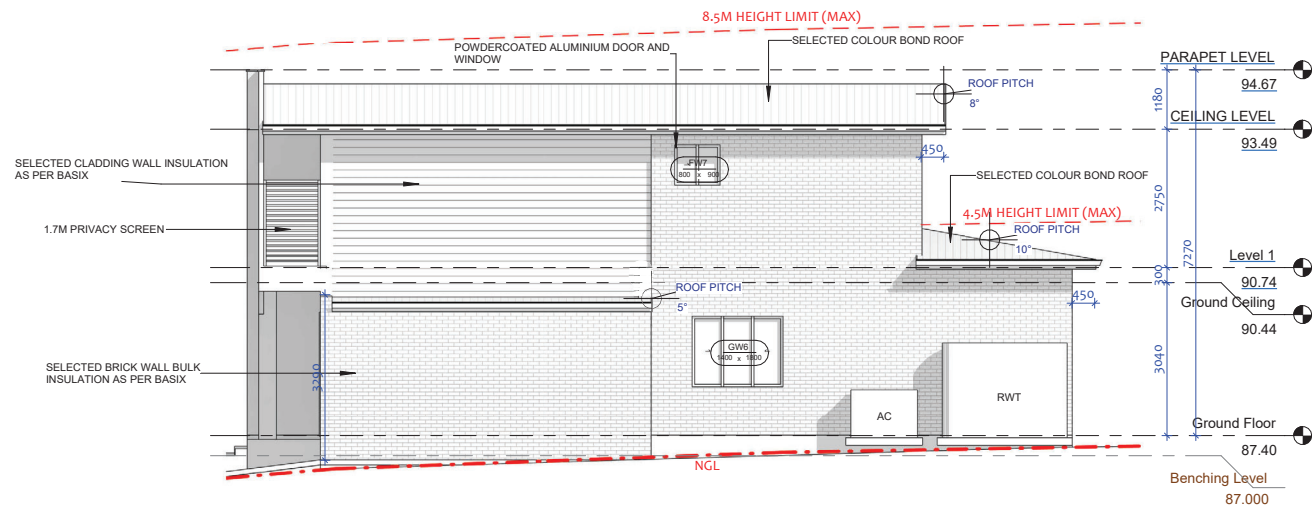

2 NORTH-EAST ELEVATION
1 : 100

CDC ISSUE

REV	DATE	DESCRIPTION	BY
3	12-06-2026	Area increased	
2	10-06-2026	Building flipped as per WAE, 230 brick wall in Garage, Garage slope made 5 degrees	
1	13-03-2026	Bank Set	

NANDI CONSTRUCTIONS

THIS DRAWING IS THE EXCLUSIVE PROPERTY OF THE DEVELOPER & THE REPRODUCTION OF ANY PART WITHOUT THE PRIOR WRITTEN CONSENT OF THE DEVELOPER IS A VIOLATION OF APPLICABLE LAWS. IN NO EVENT SHALL THE DEVELOPER BE HELD LIABLE FOR SPECIAL, COLLATERAL, INCIDENTAL OR CONSEQUENTIAL LIABILITY IN CONNECTION WITH THE USE OF THIS DIGITAL DATA, ONCE RELEASED FROM THE DEVELOPER'S OFFICE. THIS DRAWING IS TO BE READ & UNDERSTOOD IN CONJUNCTION WITH THE STRUCTURAL, MECHANICAL, ELECTRICAL & / OR ANY OTHER CONSULTANTS' DOCUMENTATION AS MAY BE APPLICABLE TO THE PROJECT PRIOR TO THE START OF ANY WORKS AND FOR ITS DURATION.

PROJECT:
LOT 124

45 MERIDIAN STREET,
LEPPINGTON

DRAWING TITLE:
ELEVATION 02

NORTH:

LOT NO: 124	DATE: 27-07-2026	SCALE: 1 : 100	DRAWING No. CDC.09	REV: 3
DRAWN BY: AS	CHECKED BY: RH			ISSUED BY:
DRAFTED BY: ID	CLIENT NAME: Owner			

DETAILS SHOWN ON THE PLANS ARE INTENDED TO BE ACCURATE. HOWEVER, BUILDER/SUPERVISOR RESERVE THE RIGHT TO ADJUST THE MEASUREMENT/ITEMS AS REQUIRED DUE TO SITE CONDITIONS.

Reference: 260043


Date: 03/08/2026

Andrew Soliman


Director/ Principal Certifier

BDC2940

Consultant who prepared this document
remains responsible for accuracy

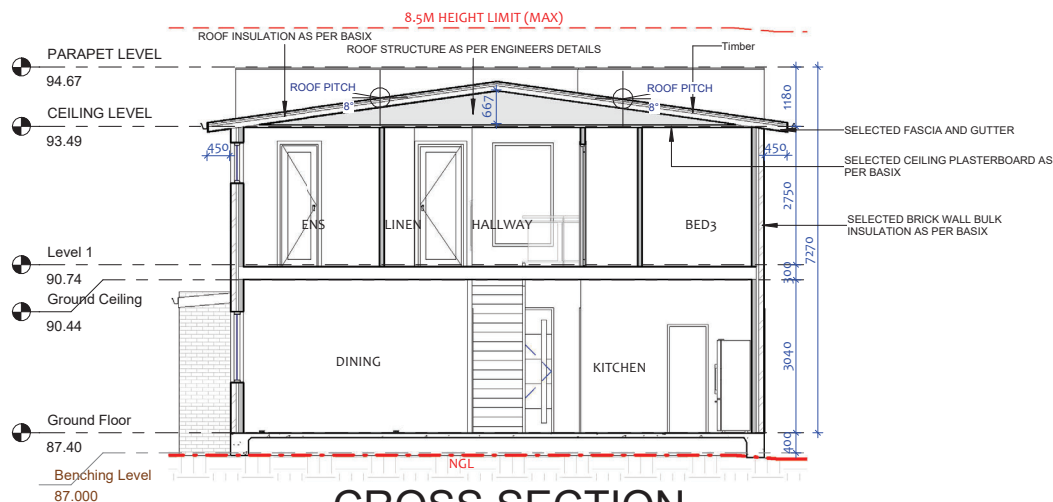

1 CROSS SECTION
1 : 100

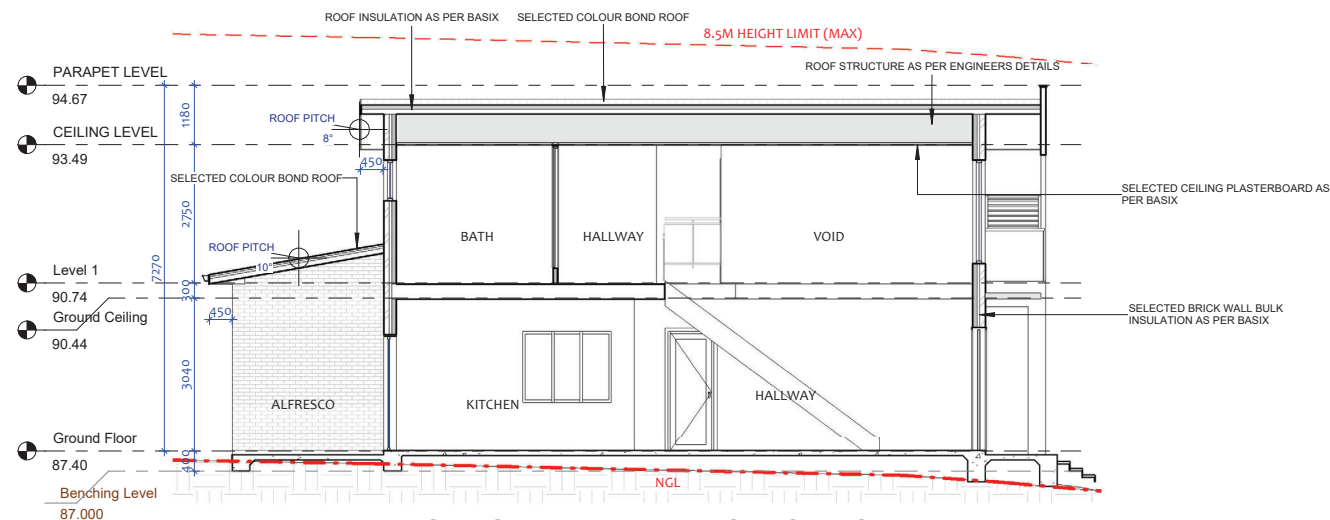

2 LONGITUDINAL SECTION
1 : 100

REV	DATE	DESCRIPTION	BY
3	12-06-2026	Area increased	
2	10-06-2026	Building flipped as per WAE, 230 brick wall in Garage, Garage slope made 5 degrees	

NANDI CONSTRUCTIONS

THIS DRAWING IS THE EXCLUSIVE PROPERTY OF THE DEVELOPER & THE REPRODUCTION OF ANY PART WITHOUT THE PRIOR WRITTEN CONSENT OF THE DEVELOPER IS A VIOLATION OF APPLICABLE LAWS. IN NO EVENT SHALL THE DEVELOPER BE HELD LIABLE FOR SPECIAL, COLLATERAL, INCIDENTAL OR CONSEQUENTIAL LIABILITY IN CONNECTION WITH THE USE OF THIS DIGITAL DATA, ONCE RELEASED FROM THE DEVELOPER'S OFFICE. THIS DRAWING IS TO BE READ & UNDERSTOOD IN CONJUNCTION WITH THE STRUCTURAL, MECHANICAL, ELECTRICAL & / OR ANY OTHER CONSULTANTS' DOCUMENTATION AS MAY BE APPLICABLE TO THE PROJECT PRIOR TO THE START OF ANY WORKS AND FOR ITS DURATION.

PROJECT:
LOT 124

45 MERIDIAN STREET,
LEPPINGTON

DRAWING TITLE:
SECTIONS

NORTH:

LOT NO:
124

DRAWN BY:
AS

DATE:
27-07-2026

CHECKED BY:
RH

SCALE:
1 : 100

DRAWING No.
CDC.10

REV:
3


ISSUED BY:

DRAFTED BY:
ID


CLIENT NAME:
Owner

CDC ISSUE

OnBuild Certifiers Pty Ltd	
Reference: 260043	
Area Schedule (Gross Building)	
Date: 03/08/2026	
Andrew Soliman	Name
Director/Principal Certifier	Area
BDC2940	
Ground Floor	
GFA	153 m ²
ALFRESCO	17 m ²
PORCH	4 m ²
Ground Floor: 3	173 m ²
Level 1	
FFA	131 m ²
BALCONY	6 m ²
Level 1: 2	137 m ²
Grand total: 5	311 m ²

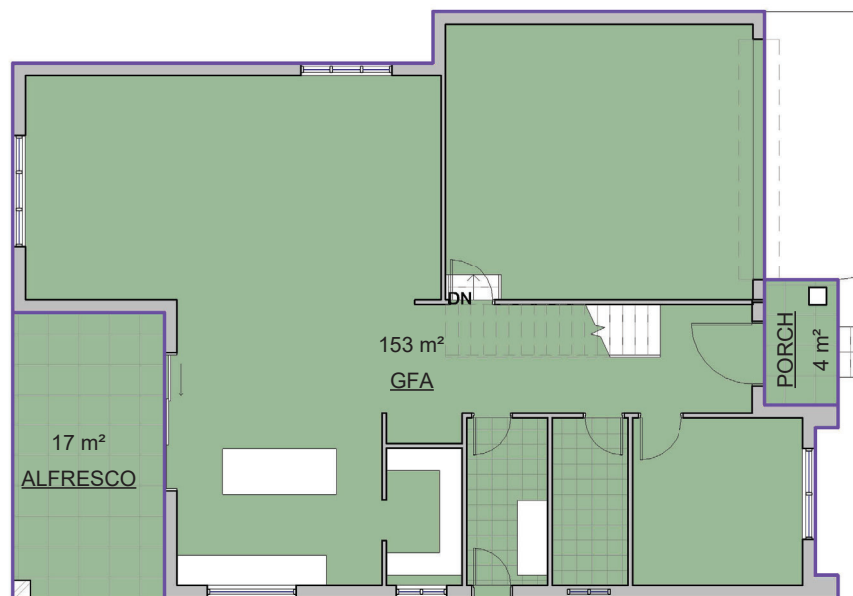

1 Ground Floor
1 : 100

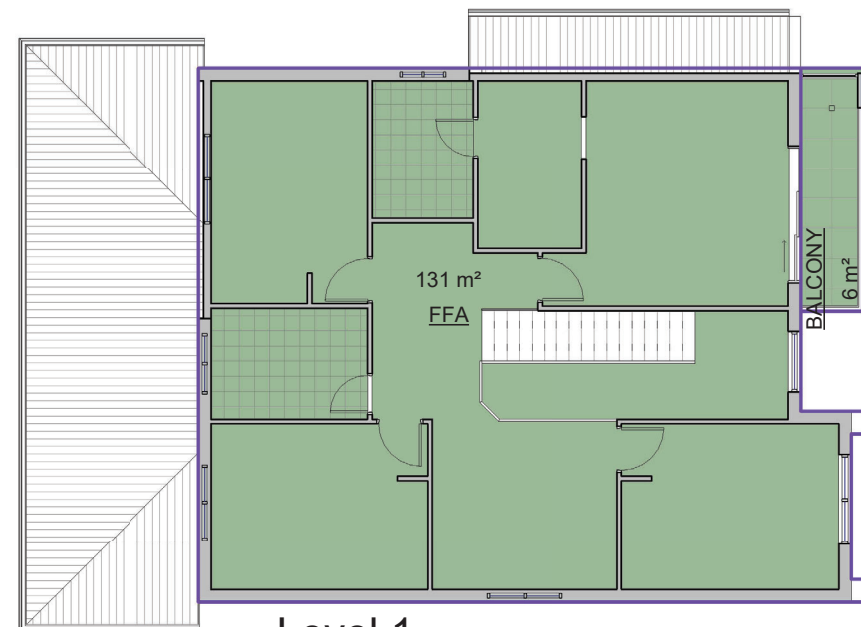

2 Level 1
1 : 100

REV	DATE	DESCRIPTION	BY
3	12-06-2026	Area increased	
2	10-06-2026	Building flipped as per WAE, 230 brick wall in Garage, Garage slope made 5 degrees	
1	13-03-2026	Bank Set	

NANDI CONSTRUCTIONS

THIS DRAWING IS THE EXCLUSIVE PROPERTY OF THE DEVELOPER & THE REPRODUCTION OF ANY PART WITHOUT THE PRIOR WRITTEN CONSENT OF THE DEVELOPER IS A VIOLATION OF APPLICABLE LAWS. IN NO EVENT SHALL THE DEVELOPER BE HELD LIABLE FOR SPECIAL, COLLATERAL, INCIDENTAL OR CONSEQUENTIAL LIABILITY IN CONNECTION WITH THE USE OF THIS DIGITAL DATA, ONCE RELEASED FROM THE DEVELOPER'S OFFICE. THIS DRAWING IS TO BE READ & UNDERSTOOD IN CONJUNCTION WITH THE STRUCTURAL, MECHANICAL, ELECTRICAL & / OR ANY OTHER CONSULTANTS' DOCUMENTATION AS MAY BE APPLICABLE TO THE PROJECT PRIOR TO THE START OF ANY WORKS AND FOR ITS DURATION.

PROJECT:
LOT 124


45 MERIDIAN STREET,
LEPPINGTON

DRAWING TITLE:
FLOOR AREA PLAN



LOT NO: 124	DATE: 27-07-2026	SCALE: 1 : 100	DRAWING No. CDC.11	REV: 3
DRAWN BY: AS	CHECKED BY: RH			ISSUED BY:
DRAFTED BY: ID	CLIENT NAME: Owner			

CDC ISSUE

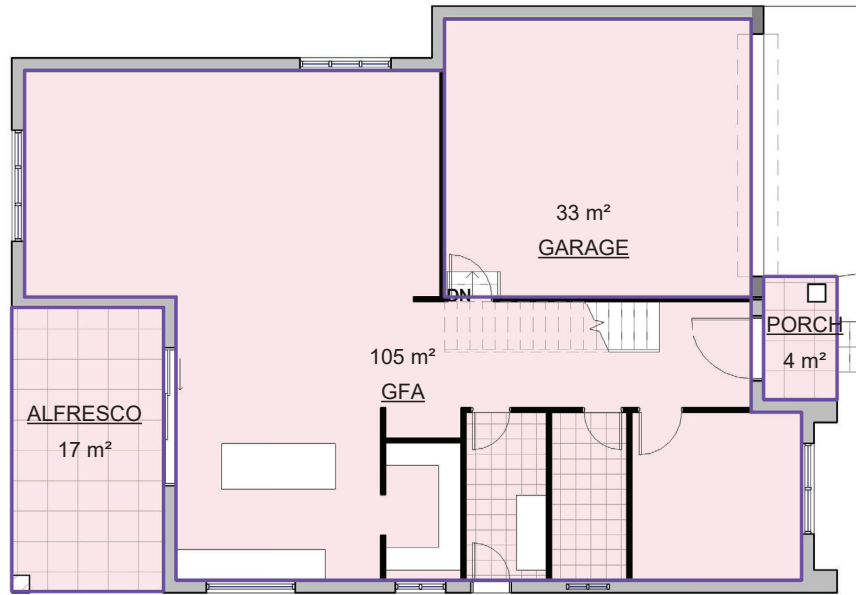

1 Ground Floor
1 : 100

OnBuild Certifiers Pty Ltd
Reference: 260043
Date: 03/08/2026
Andrew Soliman
Director/ Principal Certifier
Area Schedule (Rentable)
BDC2940
Consultant who prepared this document
remains responsible for accuracy

Ground Floor

GFA	105 m²
GARAGE	33 m²
ALFRESCO	17 m²
PORCH	4 m²


Ground Floor: 4 159 m²

Level 1

FFA	106 m²
VOID	13 m²
BALCONY	6 m²

Level 1: 3 125 m²

Grand total: 7 284 m²

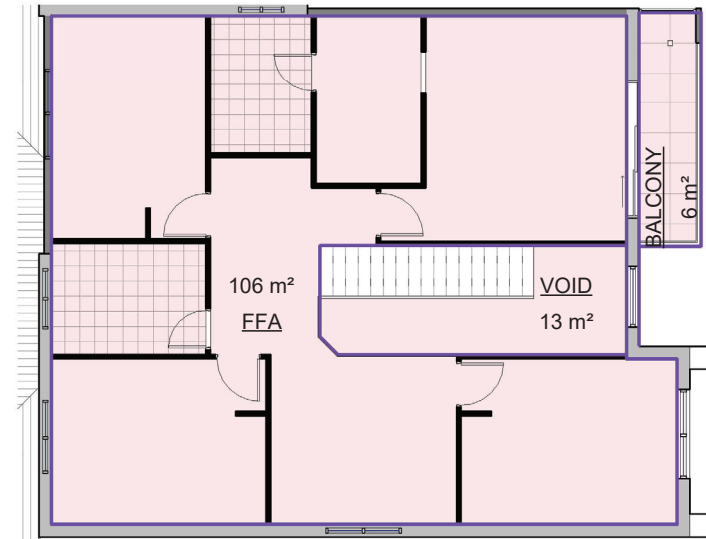

2 Level 1
1 : 100

REV	DATE	DESCRIPTION	BY
3	12-06-2026	Area increased	
2	10-06-2026	Building flipped as per WAE, 230 brick wall in Garage, Garage slope made 5 degrees	

NANDI CONSTRUCTIONS
THIS DRAWING IS THE EXCLUSIVE PROPERTY OF THE DEVELOPER & THE REPRODUCTION OF ANY PART WITHOUT THE PRIOR WRITTEN CONSENT OF THE DEVELOPER IS A VIOLATION OF APPLICABLE LAWS. IN NO EVENT SHALL THE DEVELOPER BE HELD LIABLE FOR SPECIAL, COLLATERAL, INCIDENTAL OR CONSEQUENTIAL LIABILITY IN CONNECTION WITH THE USE OF THIS DIGITAL DATA, ONCE RELEASED FROM THE DEVELOPER'S OFFICE. THIS DRAWING IS TO BE READ & UNDERSTOOD IN CONJUNCTION WITH THE STRUCTURAL, MECHANICAL, ELECTRICAL & / OR ANY OTHER CONSULTANTS' DOCUMENTATION AS MAY BE APPLICABLE TO THE PROJECT PRIOR TO THE START OF ANY WORKS AND FOR ITS DURATION.

PROJECT:
LOT 124

45 MERIDIAN STREET,
LEPPINGTON

DRAWING TITLE:
**RENTABLE AREA
PLAN**



LOT NO:
124
DRAWN BY:
AS
DRAFTED BY:
ID


DATE:
27-07-2026
CHECKED BY:
RH
CLIENT NAME:
Owner

SCALE:
1 : 100

CDC ISSUE

DRAWING No. **CDC.12** REV: **3** ISSUED BY:

OnBuild Certifiers Pty Ltd
Reference: 260043
Date: 03/08/2026
Andrew Soliman
Director/ Principal Certifier
BDC2940
Consultant who prepared this document
remains responsible for accuracy

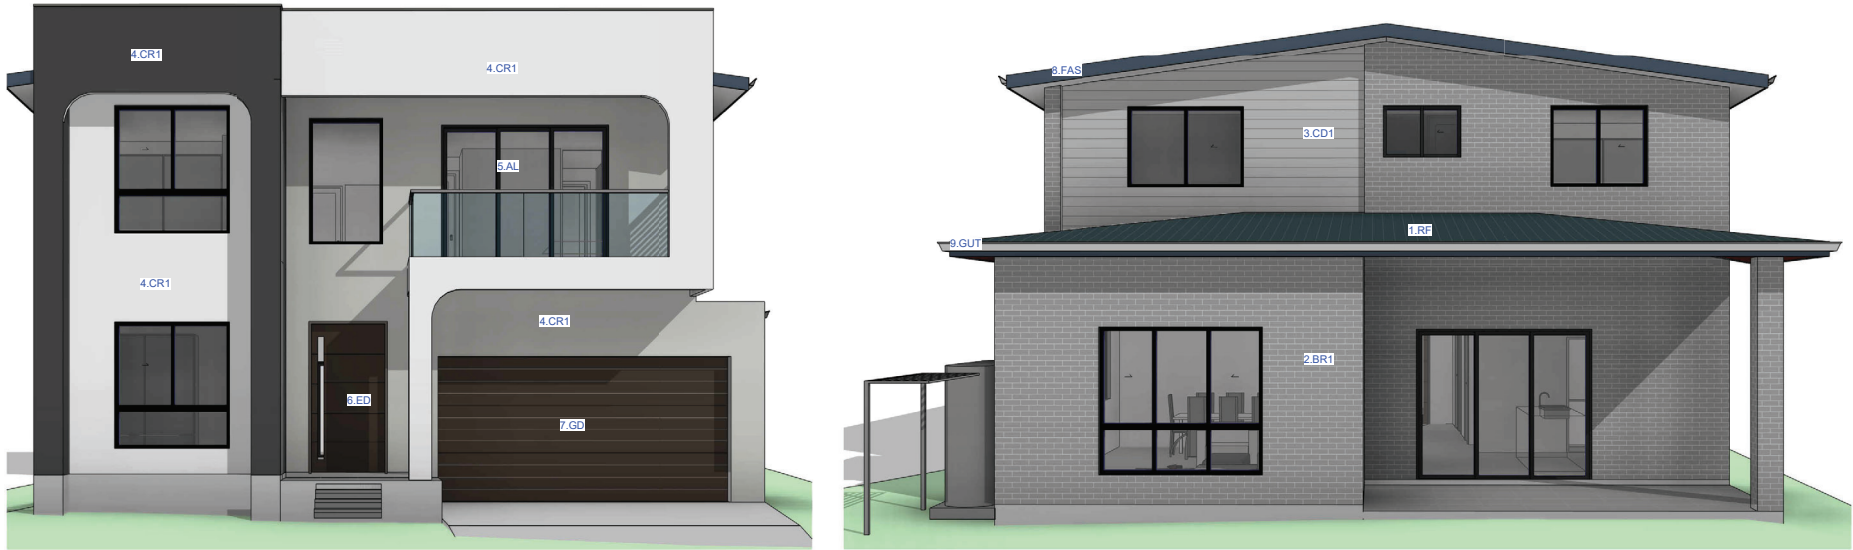

	1. RF	2. BR1	3. CD1	4. CR1	5. AL	6. ED	7. GD	8. FAS	9. GUT
	ROOF	MAIN WALLS	CLADDING	ACCENT 1/RENDER	WINDOWS/ BALUSTRADE	MAIN DOOR	GARAGE DOOR	FASCIA	GUTTER
MATERIAL	COLORBOND	BRICK	BLUEBOARD	BRICK	ALUMINIUM	TIMBER	COLORBOND	COLORBOND	COLORBOND
COLOUR									

NOTE: ALL COLOURS SPECIFIED ARE INDICATIVE ONLY AND ARE SUBJECT TO VARIATION AND TO AVAILABILITY
ANY DISCREPANCY PLEASE FOLLOW AS PER RENDERED IMAGE


REV	DATE	DESCRIPTION	BY
3	12-06-2026	Area increased	
2	10-06-2026	Building flipped as per WAE, 230 brick wall in Garage, Garage slope made 5 degrees	



THIS DRAWING IS THE EXCLUSIVE PROPERTY OF THE DEVELOPER & THE REPRODUCTION OF ANY PART WITHOUT THE PRIOR WRITTEN CONSENT OF THE DEVELOPER IS A VIOLATION OF APPLICABLE LAWS. IN NO EVENT SHALL THE DEVELOPER BE HELD LIABLE FOR SPECIAL, COLLATERAL, INCIDENTAL OR CONSEQUENTIAL LIABILITY IN CONNECTION WITH THE USE OF THIS DIGITAL DATA, ONCE RELEASED FROM THE DEVELOPER'S OFFICE. THIS DRAWING IS TO BE READ & UNDERSTOOD IN CONJUNCTION WITH THE STRUCTURAL, MECHANICAL, ELECTRICAL & / OR ANY OTHER CONSULTANTS' DOCUMENTATION AS MAY BE APPLICABLE TO THE PROJECT PRIOR TO THE START OF ANY WORKS AND FOR ITS DURATION.

PROJECT: LOT 124	DRAWING TITLE: COLOR SCHEDULE	NORTH:	LOT NO: 124	DATE: 27-07-2026	SCALE: 1 : 100	DRAWING No. CDC.14	REV: 3
45 MERIDIAN STREET, LEPPINGTON			DRAWN BY: AS	CHECKED BY: RH		ISSUED BY:	
			DRAFTED BY: ID	CLIENT NAME: Owner			

OnBuild Certifiers Pty Ltd
Reference: 260043
Date: 03/08/2026
Andrew Soliman
Director/ Principal Certifier
BDC2940
Consultant who prepared this document
remains responsible for accuracy

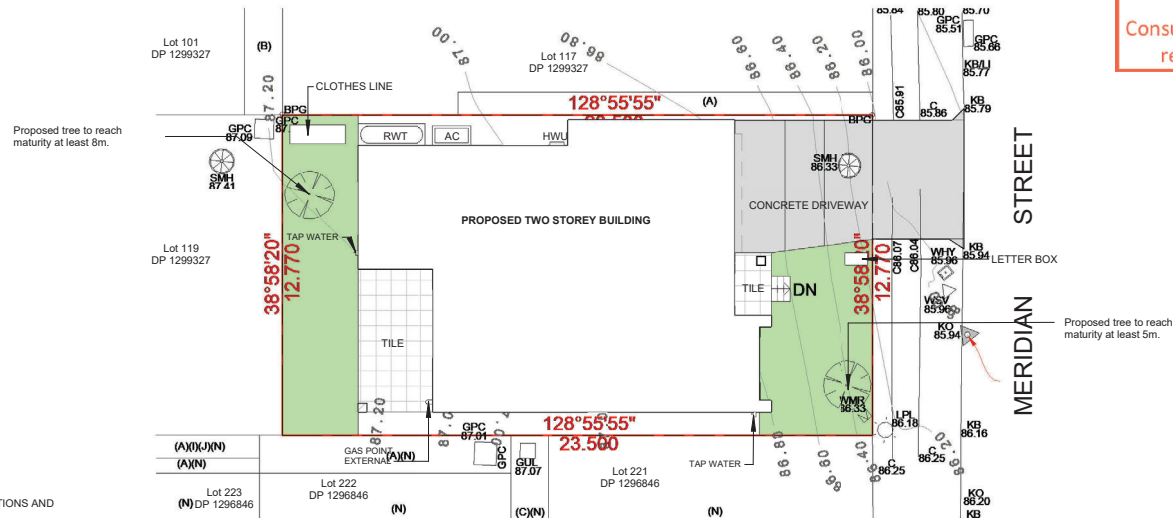

CDC - LANDSCAPE PLAN

1 : 200

GENERAL NOTES:

- LANDSCAPE CONTRACTOR TO CHECK DA CONDITIONS AND STAMPED LANDSCAPE PLAN.
- BEFORE COMMENCING WORKS TO ENSURE NO ADDITIONS/AMENDMENTS TO PLAN.
- GARDEN BEDS IN OSD BASIN TO CONSIST OF NON FLOATABLE DECORATIVE GRAVEL.
- REFER TO HYDRAULICS ENGINEERS PLAN FOR OSD DETAILS/FINAL LEVELS.
- MULCHED PLANTING BEDS TO BE A MINIMUM DEPTH OF 75mm AS SELECTED.
- CONTRACTOR'S RESPONSIBILITY TO CHECK AND ADJUST SOIL pH AS REQUIRED.
- PROVIDE TIMBER EDGE AS A MINIMUM BENEATH FENCING/GATES TO DEFINE TURF AND GARDEN BEDS/PATHWAYS.EDGING TO BE PROVIDED TO ALL AREAS WHERE DIFFERING MATERIALS MEET i.e TURF/GARDEN, TURF/GRAVEL PATH ETC.
- WEED MAT BENEATH GRAVEL PATHWAYS REQUIRED TO LIMIT MUD TRACKING.
- PREMIUM ORGANIC GARDEN MIX TO BE USED.
- ALL PLANTS TO BE HEALTHY AND VIGOROUS.
- CONTRACTOR TO MAKE GOOD TURF ON NATURE STRIP POST CONSTRUCTION.
- CONTRACTOR TO MAKE GOOD TURF ON NATURE STRIP POST CONSTRUCTION.
- DO NOT SCALE ARCHITECTURAL SETOUT FROM LANDSCAPE DRAWING.
- EXISTING TREE SPREAD APPROXIMATE ONLY.REFER TO TREE REPORT WHEN APPLICABLE.
- SITE SURVEY PROVIDED BY OTHERS.
- BUFFALO TURF PREFERRED OVER KIKUYU.

LANDSCAPE BASIX NOTE:

THE APPLICANT MUST PLANT INDIGENEOUS OR LOW WATER USE SPECIES OF VEGETATION THROUGHOUT 15 SQM OF THE SITE.

NOTE :BUILDER RESERVES THE RIGHT NOT TO UNDERTAKE NOR SUPPLY CERTIFICATE FOR OCCUPATION CERTIFICATE.


NOTE : TO AID COMPLIANCE WITH BASIX LEGISLATION,PLANTS (WHERE APPLICABLE) HAVE BEEN SELECTED FROM THE LOCAL CITY COUNCIL/SHIRE PLANT LISTS.

NOTE: LOCATION OF SEWER MAINS/LINES, WATER PIPES, UNDERGROUND ELECTRICITY AND OTHER SERVICES MUST BE OBTAINED PRIOR TO COMMENCEMENT OF ANY WORK ON SITE.

CONTRACTORS NOTE : CALCULATED AREAS DETERMINED BY CAD AND HAVE BEEN ROUNDED UP FOR USE AS A GUIDE ONLY ALLOW STANDARD PERCENTAGE FOR CUTTING AND WASTAGE .CONFIRM DIMENSIONS AND NUMBERS PRIOR TO QUOTING/ORDERING.


LANDSCAPE AREA

FRONT AREA	31.7 m ²
BACKYARD AREA	38.30 m ²
TOTAL AREA	70 m ²

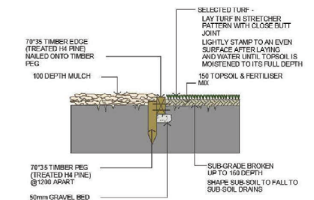

1. TURF & GARDEN EDGE DETAIL

NOTE: ALIGNMENT OF BRICK EDGE SHALL BE EVEN & FREE FROM SPLITS & HUMPS.

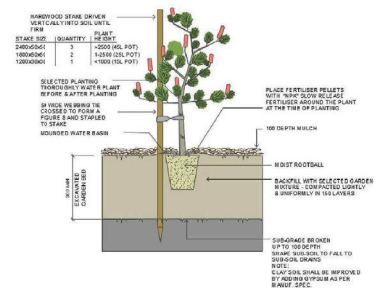

2. TREE & SHRUB PLANTING IN GARDEN BED

NOTE: DO NOT PLANT IN UNSUITABLE WEATHER CONDITIONS. DO NOT PLANT IN EXTREME HEAT, WIND, OR RAIN. CLAY SOIL IS TO BE TREATED WITH CLAY BRICKS AND ORGANIC COMPOST.

CDC ISSUE

REV	DATE	DESCRIPTION	BY
3	12-06-2026	Area increased	
2	10-06-2026	Building flipped as per WAE, 230 brick wall in Garage, Garage slope made 5 degrees	



THIS DRAWING IS THE EXCLUSIVE PROPERTY OF THE DEVELOPER & THE REPRODUCTION OF ANY PART WITHOUT THE PRIOR WRITTEN CONSENT OF THE DEVELOPER IS A VIOLATION OF APPLICABLE LAWS. IN NO EVENT SHALL THE DEVELOPER BE HELD LIABLE FOR SPECIAL, COLLATERAL, INCIDENTAL OR CONSEQUENTIAL LIABILITY IN CONNECTION WITH THE USE OF THIS DIGITAL DATA, ONCE RELEASED FROM THE DEVELOPERS OFFICE. THIS DRAWING IS TO BE READ & UNDERSTOOD IN CONJUNCTION WITH THE STRUCTURAL, MECHANICAL, ELECTRICAL & / OR ANY OTHER CONSULTANTS' DOCUMENTATION AS MAY BE APPLICABLE TO THE PROJECT PRIOR TO THE START OF ANY WORKS AND FOR ITS DURATION.

PROJECT:
LOT 124

45 MERIDIAN STREET,
LEPPINGTON

DRAWING TITLE:
LANDSCAPE PLAN

NORTH:



LOT NO:	DATE:	SCALE:	DRAWING No.	REV:
124	27-07-2026	1 : 200	CDC.15	3
DRAWN BY:	CHECKED BY:	DRAFTED BY:	CLIENT NAME:	ISSUED BY:
AS	RH	ID	Owner	

ABCB HOUSING PROVISIONS : PART 10.2 WET AREA WATERPROOFING

10.2.1 Wet Areas

- Building elements in wet areas within a building must be protected with a waterproofing system.
- The waterproofing system in (1) must be either waterproof or water resistant in accordance with 10.2.2 to 10.2.6.

10.2.2 Shower Area (enclosed and unenclosed)

- For a shower area with a hob, step-down or level threshold, the following applies:
 - The floor of the **shower area** must be **waterproof**, including any hob or step-down (see Figure 10.2.2); and
 - The walls of the **shower area** must be **waterproof** not less than 1800 mm above the floor substrate (see Figure 10.2.2).
 - Wall junctions and joints within the **shower area** must be **waterproof** not less than 40 mm either side of the junction (see Figure 10.2.2).
 - Wall/floor junctions within the shower area must be **waterproof** (see Figure 10.2.2).
- Penetrations within the shower area must be **waterproof**.
- A shower with a **preformed shower base** must also comply with the requirements of (1), except for (a) which is not applicable.

Figure 10.2.2: Extent of treatment for shower areas - concrete compressed fibre-cement and fibre-cement sheet floors.

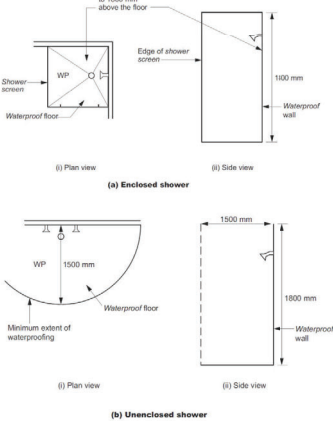


Figure Notes
 Wall/floor junction heights are to be as per 10.2.2 to 10.2.6 (as applicable).

Notes
 Where a shower is above a bath or spa, use requirements for shower.

10.2.3 Area outside shower area

- For concrete, compressed fibre-cement and fibre-cement sheet flooring, the floor of the room must be water resistant.
- For timber floors including particleboard, plywood and other timber based flooring materials, the floor of the room must be waterproof.
- Wall/floor junctions must be -
 - waterproof, and
 - where a flashing is used, the horizontal leg must be not less than 40 mm.

10.2.4 Areas adjacent to baths and spas without showers

- For areas adjacent to all baths and spas, the following applies:
 - For concrete, compressed fibre-cement and fibre-cement sheet flooring, the floor of the room must be water resistant.
 - For timber floors including particleboard, plywood and other timber based flooring materials, the floor of the room must be waterproof.
- For areas adjacent to non-freestanding baths and spas, the following applies:
 - Walls must be water resistant (see Figure 10.2.4a and Figure 10.2.4b)-
 - to a height of not less than 150mm above the vessel, for the extent of the vessel, where the vessel is within 75mm of a wall and
 - for all exposed surfaces below vessel lip.
 - Wall junctions and joints must be water resistant within 150mm above a vessel for the extent of the vessel.
 - Wall/floor junctions must be waterproof for the extent of the vessel (see Figure 10.2.4a and Figure 10.2.4b).
- For inserted baths and spas, the following applies.
 - For floors and horizontal surfaces:
 - Any shelf area adjoining the bath or spa must be waterproof and include a waterstop under the vessel lip.
 - There are no requirements for the floor under a bath or spa.
 - For walls:
 - Waterproof to not less than 150mm above the lip of a bath or spa.
 - There are no requirements for the floor under a bath or spa.
 - For wall junctions and joints, the following applies:
 - Waterproof junctions within 150mm of a bath or spa.
 - There are no requirements for junctions and joints in walls beneath the lip of a bath or spa.
 - Tap and spout penetrations must be waterproof where they occur in horizontal surfaces.

Figure 10.2.4a: Areas adjacent to baths and spas without showers for concrete, compressed fibre-cement and fibre-cement sheet flooring




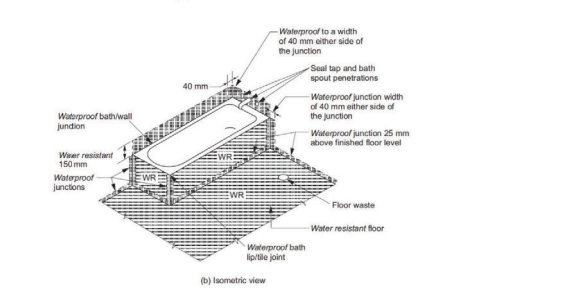



Figure 10.2.4b: Areas adjacent to baths and spas without showers for timber floors including particle-board, plywood and other floor materials

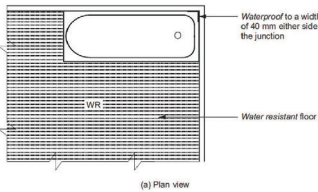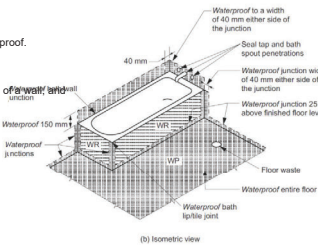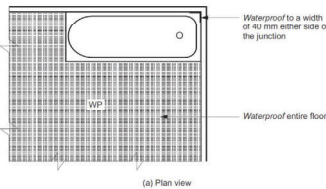

10.2.5 Other areas

- For walls adjoining other types of vessels (not sink, bath or shower) (b), the following applies:
 - Walls must be water resistant to a height of not less than 150mm above the vessel, for the extent of the vessel, where the vessel is within 75 mm of a wall (see Figure 10.2.5.)
 - Waterproof wall/floor junctions must be water resistant.
 - Waterproof tap and spout penetrations where they occur in surfaces required to be waterproof or water resistant.
- For laundries and WCs, the following applies:
 - The floor of the room must be water resistant.
 - Wall/floor junctions must be water resistant, and where a flashing is used, the horizontal leg must be not less than 40 mm.
- For WCs with a handheld bidet spray installation, the following applies:
 - The floor of the room must be waterproof.
 - Walls must be -
 - waterproof in WC area within a 900 mm radius from the wall connection of the handheld bidet spray device to a height of not less than 150mm above the floor substrate; and
 - water resistant in WC area within a 900 mm radius from the wall connection of the handheld bidet device to not less than 1200 mm above the finished floor level of the WC.
 - Wall junctions within the WC area within 900 mm radius from the wall connection of the handheld bidet spray device must be waterproof.
 - Wall/floor junctions within the WC area within 1000 mm radius from the wall connection of the handheld bidet spray device must be waterproof.
 - Penetrations in the WC area must be waterproof.

Figure 10.2.5: Bath and vessel abutting wall - areas to be protected

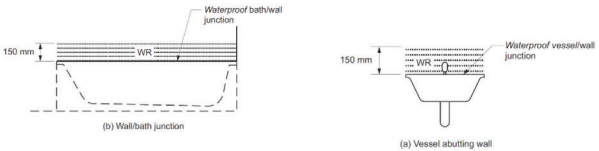

10.2.6 Waterproofing systems

- For the purposes of this Part, a waterproofing system is deemed -
 - waterproof, if it complies with (2); or
 - water resistant, if it complies with (3).
- For a waterproofing system required to be waterproof in accordance with 10.2.2 to 10.2.5, the materials nominated in 10.2.8 must be used.
- For a waterproofing system required to be water resistant in accordance with 10.2.2 to 10.2.5, the materials nominated in 10.2.9 must be used in conjunction with the materials in 10.2.10.

10.2.12 Construction of wet area floors - falls

Where a floor waste is installed -

- the minimum continuous fall of a floor plane to the waste must be 1:80; and
- the maximum continuous fall of a floor plane to the waste must be 1:50.

3	12-06-2026	Area increased		
2	10-06-2026	Building flipped as per WAE, 230 brick wall in Garage, Garage slope made 5 degrees		
REV	DATE	DESCRIPTION		BY

THIS DRAWING IS THE EXCLUSIVE PROPERTY OF THE DEVELOPER & THE REPRODUCTION OF ANY PART WITHOUT THE PRIOR WRITTEN CONSENT OF THE DEVELOPER IS A VIOLATION OF APPLICABLE LAWS. IN NO EVENT SHALL THE DEVELOPER BE HELD LIABLE FOR SPECIAL, COLLATERAL, INCIDENTAL OR CONSEQUENTIAL LIABILITY IN CONNECTION WITH THE USE OF THIS DIGITAL DATA, ONCE RELEASED FROM THE DEVELOPER'S OFFICE. THIS DRAWING IS TO BE READ & UNDERSTOOD IN CONJUNCTION WITH THE STRUCTURAL, MECHANICAL, ELECTRICAL & / OR ANY OTHER CONSULTANTS' DOCUMENTATION AS MAY BE APPLICABLE TO THE PROJECT PRIOR TO THE START OF ANY WORKS AND FOR ITS DURATION.

PROJECT:

LOT 124

45 MERIDIAN STREET, LEPPINGTON

DRAWING TITLE:

WATERPROOFING DETAILS

NORTH:

LOT NO: 124

DRAWN BY: AS

DRAFTED BY: ID

DATE: 27-07-2026

CHECKED BY: RH

CLIENT NAME: Owner

SCALE: 1 : 50

DRAWING No. CDC.16

REV: 3

ISSUED BY: