

FOR CONSTRUCTION

LOT 2088 13 LORIKEET STREET WILTON

PROPOSED CONSTRUCTION OF A TWO STOREY DWELLING



BASIX COMMITMENTS		Certificate number: 1860692S_02 Date of issue: Wednesday, 12 August 2026
WATER		
LANDSCAPE	136m2	
TOILETS	4 STARS	
KITCHEN TAPS	5 STARS	
SHOWER HEADS	4 STAR (>6 but <=7.5 Umin)	
BASIN TAPS	4 STARS	
ALTERNATIVE WATER	Reticulated Alternative Water Supply	
ALT. WATER USES - RETIC	ALL TOILETS + ONE OUTDOOR TAP	
SWIMMING POOL	N/A	
ENERGY		
HOT WATER	Electric Heat Pump - 36 to 40 STCs or better	
AIR-CON (HEATING)	3 PHASE DUCTED - EER 3.0-3.5	
AIR-CON (COOLING)	3 PHASE DUCTED - EER 3.0-3.5	
VENTILATION - BATHROOM	INTERLOCKED WITH LIGHT	
VENTILATION - KITCHEN	DUCTED - MANUAL SWITCH	
VENTILATION - LAUNDRY	NONE/ NATURAL VENTILATION	
PV SYSTEM	6.6 KW, install at 10-25deg north east	
COOKTOP	GAS	
OVEN	ELECTRIC	
CLOTHES DRYING	OUTDOOR CLOTHESLINE	
LIGHTING	DEDICATED LED	

GENERAL LEGEND	
AC	AIR CONDITIONING UNIT
AL	POWDERCOATED ALUMINIUM DOOR/ WINDOW
BAL	BALUSTRADE TYPE
BG	BOX GUTTER
BR1, BR2, etc.	BRICK FACE TYPE
CAP	METAL CAPPING
CD1, CD2, etc.	WALL CLADDING
CONC.	CONCRETE FLOOR
CPT	CARPET
CRT	CONCRETE ROOF TILES
CR1, CR2, etc.	CEMENT RENDER TYPE/ COLOUR
DP/S	DOWN PIPE
DW	DISH WASHER
ED	ENTRY DOOR
F	FRIDGE
FAS	FASCIA
FET	FEATURE TILE
FT, FT1, FT2, etc.	FLOOR TILES
FW	FLOOR WASTE
GD	GARAGE DOOR
GUT	GUTTER
HWU	HOT WATER UNIT
HYB	HYBRID FLOOR
L	LINEN
MR	METAL ROOF
MW	MICROWAVE OVEN
NGL	NATURAL GROUND LEVEL
OBS	OBSCURED GLASS
P	PANTRY
R	ROBE
RL	REDUCED LEVEL
RWH	RAIN WATER HEAD
RWT	RAIN WATER TANK
S	STORAGE
TOW	TOP OF WALL
TL	TIMBER LAMINATE
WC	WATER CLOSET
WM	WASHING MACHINE
SD	SMOKE DETECTOR

Sheet List		
Sheet No.	Sheet Name	Revision
CDC.01	COVER SHEET	11
CDC.02A	GENERAL NOTES	5
CDC.02B	GENERAL NOTES	5
CDC.03	LOCATION PLAN AND SITE PLAN	6
CDC.04	SITE ANALYSIS AND SEDIMENT CONTROL	6
CDC.05	GROUND FLOOR PLAN	11
CDC.06	FIRST FLOOR LEVEL	11
CDC.07	ROOF PLAN	8

Sheet List		
Sheet No.	Sheet Name	Revision
CDC.08	ELEVATION 01	11
CDC.09	ELEVATION 02	7
CDC.10	SECTIONS	6
CDC.11	FLOOR AREA PLAN	6
CDC.12	RENTABLE AREA PLAN	6
CDC.14	COLOR SCHEDULE	11
CDC.15	LANDSCAPE PLAN	6
CDC.16	WATERPROOFING DETAILS	5

NOTE.: ALL IMAGES ARE FOR ILLUSTRATION ONLY AND ARE SUBJECT TO VARIATION AND TO AVAILABILITY OF MATERIALS.

11				CDC ISSUE			
11	Date 11	Glass railing at balcony, LP gas - Ekta/Client		LOT NO:	DATE:	SCALE:	DRAWING No: REV: 11
10	30-07-2026	Metal Railing on Balcony - Developer/Client		2088	20-08-2026	As indicated	CDC.01
9	28-07-2026	Full Cladding on Front facade on first floor - Bishwas		DRAWN BY:	CHECKED BY:		ISSUED BY:
8	27-07-2026	Facade Updated with stone and wooden cladding - Bishwas/Sheela		AS	RH		
7	16-07-2026	Metal Railings on balcony - Ekta		DRAFTED BY:	CLIENT NAME:		
REV	DATE	DESCRIPTION	BY	SL	Bhasker Maskey & Sabnam Karki		



THIS DRAWING IS THE EXCLUSIVE PROPERTY OF THE DEVELOPER & THE REPRODUCTION OF ANY PART WITHOUT THE PRIOR WRITTEN CONSENT OF THE DEVELOPER IS A VIOLATION OF APPLICABLE LAWS. IN NO EVENT SHALL THE DEVELOPER BE HELD LIABLE FOR SPECIAL COLLATERAL, INCIDENTAL OR CONSEQUENTIAL LIABILITY IN CONNECTION WITH THE USE OF THIS DIGITAL DATA ONCE RELEASED FROM THE DEVELOPER'S OFFICE. THIS DRAWING IS TO BE READ & UNDERSTOOD IN CONJUNCTION WITH THE STRUCTURAL, MECHANICAL, ELECTRICAL & / OR ANY OTHER CONSULTANT'S DOCUMENTATION AS MAY BE APPLICABLE TO THE PROJECT PRIOR TO THE START OF ANY WORKS AND FOR ITS DURATION.

BUILDING SPECIFICATIONS

**National Construction Code – Volume 2,
Amendment 1 – Building Code of Australia 2022
& Housing Provisions Standard 2022**

SITE PREPARATION

- PART 3.1 OF THE NCC VOLUME 2, AMENDMENT 1 - BUILDING CODE OF AUSTRALIA 2022 & HOUSING PROVISIONS STANDARD 2022.

EARTHWORKS

- TO BE CARRIED OUT IN ACCORDANCE WITH THE REQUIREMENTS OF THE ENVIRONMENTAL PLANNING & ASSESSMENT ACT 1979 AND DEVELOPMENT CONSENT CONDITIONS
- PART 3.2 OF THE NCC VOLUME 2, AMENDMENT 1 - BUILDING CODE OF AUSTRALIA 2022 & HOUSING PROVISIONS STANDARD 2022.
- AS 4678:2002 - EARTH-RETAINING STRUCTURES

DRAINAGE

- PART 3.3 OF THE NCC VOLUME 2, AMENDMENT 1 - BUILDING CODE OF AUSTRALIA 2022 & HOUSING PROVISIONS STANDARD 2022.
- AS/NZS 3500.1:2021 - PLUMBING & DRAINAGE - WATER SERVICES
- AS/NZS 3500.2:2021 - PLUMBING & DRAINAGE - SANITARY PLUMBING & DRAINAGE
- AS/NZS 3500.3:2021 - PLUMBING & DRAINAGE STORMWATER DRAINAGE
- AS/NZS 3500.4:2021 - PLUMBING & DRAINAGE - HEATED WATER SERVICES

STRUCTURAL WORK

- Part 2.2 OF THE NCC VOLUME 2, AMENDMENT 1 - BUILDING CODE OF AUSTRALIA 2022 & HOUSING PROVISIONS STANDARD 2022.
- AS 4100-2020- STEEL STRUCTURES CODES
- AS/NZS 1170.0-2002 – GENERAL PRINCIPLES
- AS/NZS 1170.1-2002 – PARTS 1 PERMANENT, IMPOSED AND OTHER ACTIONS
- AS/NZS 1170.2-2021 – PART 2 WIND ACTIONS
- AS 3700-2018– SAA MASONRY CODE
- AS 1684.3-2021- RESIDENTIAL TIMBER FRAMED CONSTRUCTION

FOOTINGS & SLABS

- PART 4 OF THE NCC VOLUME 2, AMENDMENT 1 - BUILDING CODE OF AUSTRALIA 2022 & HOUSING PROVISIONS STANDARD 2022.
- AS 2159:2009 - PILING - DESIGN & INSTALLATION
- AS 2870:2011 - RESIDENTIAL SLABS & FOOTINGS
- AS 3600:2018 - CONCRETE STRUCTURES

MASONRY

- PART 5 OF THE NCC VOLUME 2, AMENDMENT 1 - BUILDING CODE OF AUSTRALIA 2022 & HOUSING PROVISIONS STANDARD 2022.
- AS 3700:2018 - MASONRY STRUCTURES
- PART 6 OF THE NCC VOLUME 2, AMENDMENT 1 - BUILDING CODE OF AUSTRALIA 2022 & HOUSING PROVISIONS STANDARD 2022.
- AS 1684.2:2021 - RESIDENTIAL TIMBER-FRAMED CONSTRUCTION - NON- CYCLONIC AREAS
- AS 1720.1:2010 - TIMBER STRUCTURES - DESIGN METHODS
- AS 4100:2020 - STEEL STRUCTURES
- AS 3660.1-2014 – TERMITE MANAGEMENT SYSTEM

ROOF & WALL CLADDING

- PART 7 OF THE NCC VOLUME 2, AMENDMENT 1 - BUILDING CODE OF AUSTRALIA 2022 & HOUSING PROVISIONS STANDARD 2022.
- AS 1273:1991 - UNPLASTICIZED PVC (UPVC) DOWNPIPES & FITTINGS FOR RAINWATER
- AS 1562.1:2018 - DESIGN & INSTALLATION OF SHEET ROOF & WALL CLADDING - METAL
- AS/NZS 1562.3:2006 - DESIGN & INSTALLATION OF SHEET ROOF & WALL CLADDING - PLASTIC
- AS 2049:2002 - ROOF TILES
- AS 2050:2018 - INSTALLATION OF ROOF TILES
- AS 4285:2019 – ROOFLIGHTS

GLAZING

- PART 8 OF THE NCC VOLUME 2, AMENDMENT 1 - BUILDING CODE OF AUSTRALIA 2022 & HOUSING PROVISIONS STANDARD 2022.
- AS 1288:2021 - GLASS IN BUILDINGS -SELECTION & INSTALLATION
- AS 2047:2014 - WINDOWS & EXTERNAL GLAZED DOORS IN BUILDINGS
- AS/NZS 2208:1996 - SAFETY GLAZING MATERIALS IN BUILDINGS

FIRE SAFETY

- PART 9 OF THE NCC VOLUME 2, AMENDMENT 1 - BUILDING CODE OF AUSTRALIA 2022 & HOUSING PROVISIONS STANDARD 2022.
- AS 3786:2014 - SMOKE ALARMS USING SCATTERED LIGHT, TRANSMITTED LIGHT OR IONIZATION

HEALTH & AMENITY

- PART 10 OF THE NCC VOLUME 2, AMENDMENT 1 - BUILDING CODE OF AUSTRALIA 2022 & HOUSING PROVISIONS STANDARD 2022.
- AS/NZS ISO 717.1:2004 - ACOUSTICS - RATING OF SOUND INSULATION IN BUILDINGS & OF BUILDING ELEMENTS -AIRBORNE SOUND INSULATION
- AS ISO 717.2:2004 - ACOUSTICS - RATING OF SOUND INSULATION IN BUILDINGS & OF BUILDING ELEMENTS - IMPACT SOUND INSULATION
- AS 1668.2:2012 - THE USE OF VENTILATION & AIR CONDITIONING IN BUILDINGS - MECHANICAL VENTILATION IN BUILDINGS
- AS 1668.4:2012 - THE USE OF VENTILATION & AIR CONDITIONING IN BUILDINGS - NATURAL VENTILATION OF BUILDINGS
- AS/NZS 1680.0:2009 - INTERIOR LIGHTING - SAFE MOVEMENT
- AS 3740:2021 - WATERPROOFING OF DOMESTIC WET AREAS
- AS 3000-2018 – ELECTRICAL INSTALLATION
- BCA Part 10.8.1, AS4200.1 & AS4200.2 – PLIABLE BUILDING MEMBRANE INSTALLED.

WATERPROOFING

- PART 10.2 OF THE NCC VOLUME 2, AMENDMENT 1 - BUILDING CODE OF AUSTRALIA 2022 & HOUSING PROVISIONS STANDARD 2022
- AS 3740-2021– WATERPROOFING TO WET AREA
- AS 4654-2012 – EXTERNAL WET AREAS

SAFE MOVEMENT & ACCESS

- PART 11 OF THE NCC VOLUME 2, AMENDMENT 1 - BUILDING CODE OF AUSTRALIA 2022 & HOUSING PROVISIONS STANDARD 2022.
- AS 1428.1:2009 - DESIGN FOR ACCESS & MOBILITY – GENERAL REQUIREMENTS FOR ACCESS - NEW BUILDING WORK
- AS 1657:2018 - FIXED PLATFORMS, WALKWAYS, STAIRWAYS & LADDERS - DESIGN, CONSTRUCTION & INSTALLATION

HANDRAILS & BALUSTRADE

- PART 11.3.3 OF THE NCC VOLUME 2, AMENDMENT 1 - BUILDING CODE OF AUSTRALIA 2022 & HOUSING PROVISIONS STANDARD 2022.
- PART 11.3.4 OF THE NCC VOLUME 2, AMENDMENT 1 - BUILDING CODE OF AUSTRALIA 2022 & HOUSING PROVISIONS STANDARD 2022.
- PART 11.3.5 OF THE NCC VOLUME 2, AMENDMENT 1 - BUILDING CODE OF AUSTRALIA 2022 & HOUSING PROVISIONS STANDARD 2022.
- AS 1170.1-2002 – BALUSTRADE INSTALLATION

PROTECTION OF OPENABLE WINDOW

PART 11.3.7 AND 11.3.8 OF THE NCC VOLUME 2, AMENDMENT 1 - BUILDING CODE OF AUSTRALIA 2022 & HOUSING PROVISIONS STANDARD 2022.

ENERGY EFFICIENCY

- PART 13 OF THE NCC VOLUME 2, AMENDMENT 1 - BUILDING CODE OF AUSTRALIA 2022 & HOUSING PROVISIONS STANDARD 2022 & BASIX CERTIFICATE.

MECHANICAL VENTILATION

- EXHAUST FROM A BATHROOM, SANITARY COMPARTMENT TO DISCHARGE DIRECTLY TO OUTDOOR AIR WITH MINIMUM FLOW RATE OF 25L/S & MAKE-UP AIR VIA OPENINGS TO AN ADJACENT ROOM WITH A FREE AREA OF 14,000 MM². THIS EXHAUST SYSTEM MUST BE INTERLOCKED WITH LIGHT SWITCH AND INCLUDE RUN-ON TIMER SO THAT THE EXHAUST SYSTEM CONTINUES TO OPERATE FOR 10 MINUTES AFTER THE LIGHT SWITCH IS OFF.
- ANY INSTALLED - KITCHEN RANGEHOOD EXHAUST TO DISCHARGE DIRECTLY OR VIA DUCT TO OUTDOOR AIR WITH MINIMUM FLOW RATE OF 40L/S & MAKE-UP AIR VIA OPENINGS TO AN ADJACENT ROOM WITH A FREE AREA OF 14,000 MM².
- LAUNDRY EXHAUST TO DISCHARGE DIRECTLY OR VIA DUCT TO OUTDOOR AIR WITH MINIMUM FLOW RATE OF 40L/S & MAKE-UP AIR VIA OPENINGS TO AN ADJACENT ROOM WITH A FREE AREA OF 14,000 MM².



REV	DATE	DESCRIPTION	BY
5	25-06-2026	CDC ISSUE	

THIS DRAWING IS THE EXCLUSIVE PROPERTY OF THE DEVELOPER & THE REPRODUCTION OF ANY PART WITHOUT THE PRIOR WRITTEN CONSENT OF THE DEVELOPER IS A VIOLATION OF APPLICABLE LAWS. IN NO EVENT SHALL THE DEVELOPER BE HELD LIABLE FOR SPECIAL COLLATERAL, INCIDENTAL OR CONSEQUENTIAL LIABILITY IN CONNECTION WITH THE USE OF THIS DIGITAL DATA ONCE RELEASED FROM THE DEVELOPER'S OFFICE. THIS DRAWING IS TO BE READ & UNDERSTOOD IN CONJUNCTION WITH THE STRUCTURAL, MECHANICAL, ELECTRICAL & / OR ANY OTHER CONSULTANT'S DOCUMENTATION AS MAY BE APPLICABLE TO THE PROJECT PRIOR TO THE START OF ANY WORKS AND FOR ITS DURATION.

PROJECT:
Lot 2088 13 LORIKEET STREET
13 LORIKEET STREET WILTON

DRAWING TITLE:
GENERAL NOTES

<u>NORTH:</u>	LOT NO:	DATE:	SCALE:	DRAWING No:	REV:
	2088	20-08-2026	1 : 2	CDC.02A	5
	DRAWN BY:	CHECKED BY:			ISSUED BY:
	AS	RH			
	DRAFTED BY:	CLIENT NAME:			
	SL	Bhasker Maskey & Sabnam Karki			

CDC ISSUE

DRAWING No: 5

ISSUED BY:

TERMITE SHEET


- TERMITE SHEET EXTENDS THROUGH THE ENTIRE MASONRY LEAF AND IS VISIBLE AT THE FINISHED FACE OF THE WALL.



FIGURE 5.5 (in part) TYPICAL SHEET INSTALLATION TO EXTERNAL WALL WITH CONCRETE FLOOR SLAB



DPC FOR BRICKS

DAMP-PROOF COURSE (DPC) TO EXTENDS THROUGH THE ENTIRE MASONRY LEAF AND NEED TO BE VISIBLE AT THE FINISHED FACE OF THE WALL FROM OUTSIDE

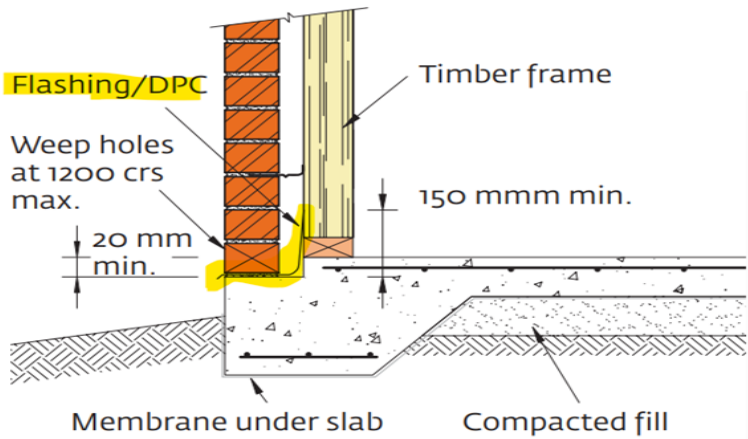

OVERFLOW TO BALCONY:

- SURFACE DRAIN & OVERFLOW TO BALCONY

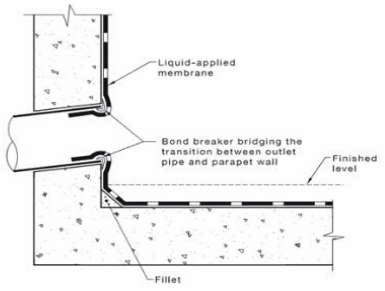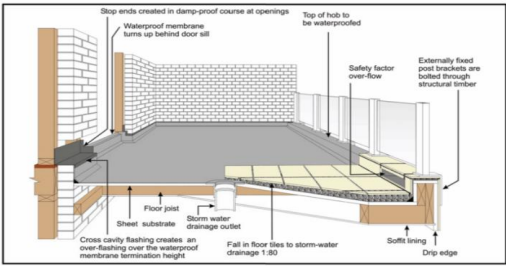

(a) Overflow through parapet

WATERPROOFING

FALL TO FLOOR WASTE TO BE MINIMUM 1:80 TO MAXIMUM 1:50

Figure 10.2.29: Typical membrane termination at drainage outlet



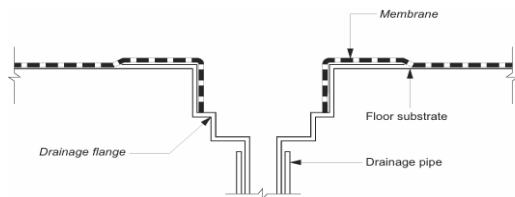


Figure 10.2.24: Typical bathroom door details for whole bathroom waterproofing

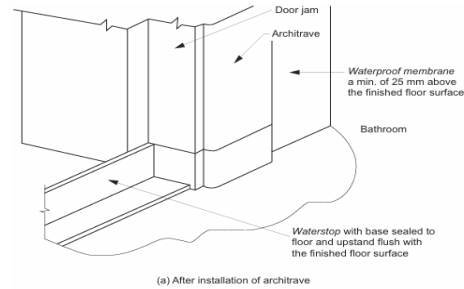

(a) After installation of architrave

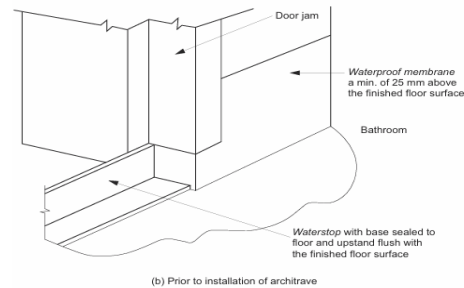


(b) Prior to installation of architrave


BASIN & BATHTUB:

Figure 10.2.5:

Bath and vessel abutting wall — areas to be protected

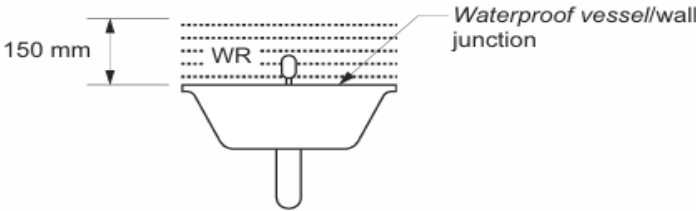

(a) Vessel abutting wall

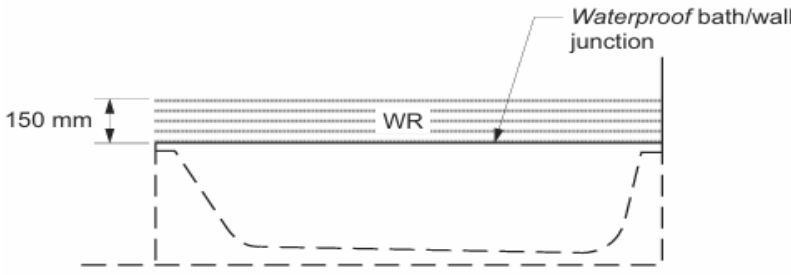


(b) Wall/bath junction


ENCLOSED SHOWER AREA

Figure 10.2.17:

Typical hobless construction

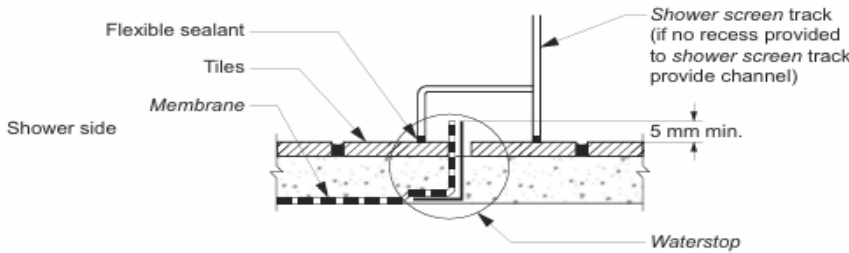

Extent of treatment for shower areas — concrete compressed fibre-cement and fibre-cement sheet floors

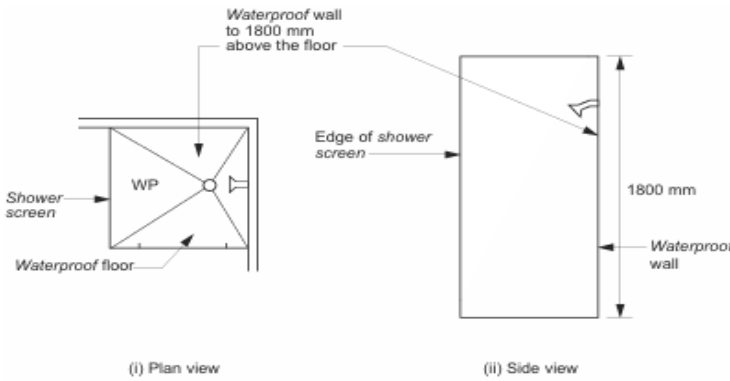

(i) Plan view

(ii) Side view

(a) Enclosed shower

REV	DATE	DESCRIPTION	BY
5	25-06-2026	CDC ISSUE	




THIS DRAWING IS THE EXCLUSIVE PROPERTY OF THE DEVELOPER & THE REPRODUCTION OF ANY PART WITHOUT THE PRIOR WRITTEN CONSENT OF THE DEVELOPER IS A VIOLATION OF APPLICABLE LAWS. IN NO EVENT SHALL THE DEVELOPER BE HELD LIABLE FOR SPECIAL COLLATERAL, INCIDENTAL OR CONSEQUENTIAL LIABILITY IN CONNECTION WITH THE USE OF THIS DIGITAL DATA ONCE RELEASED FROM THE DEVELOPER'S OFFICE. THIS DRAWING IS TO BE READ & UNDERSTOOD IN CONJUNCTION WITH THE STRUCTURAL, MECHANICAL, ELECTRICAL & / OR ANY OTHER CONSULTANT'S DOCUMENTATION AS MAY BE APPLICABLE TO THE PROJECT PRIOR TO THE START OF ANY WORKS AND FOR ITS DURATION.

PROJECT:
Lot 2088 13 LORIKEET STREET
13 LORIKEET STREET WILTON


DRAWING TITLE:
GENERAL NOTES

NORTH:

CDC ISSUE			
LOT NO: 2088	DATE: 20-08-2026	SCALE: 1 : 2	DRAWING No: REV: 5
DRAWN BY: AS	CHECKED BY: RH	CDC.02B	
DRAFTED BY: SL	CLIENT NAME: Bhasker Maskey & Sabnam Karki	ISSUED BY:	

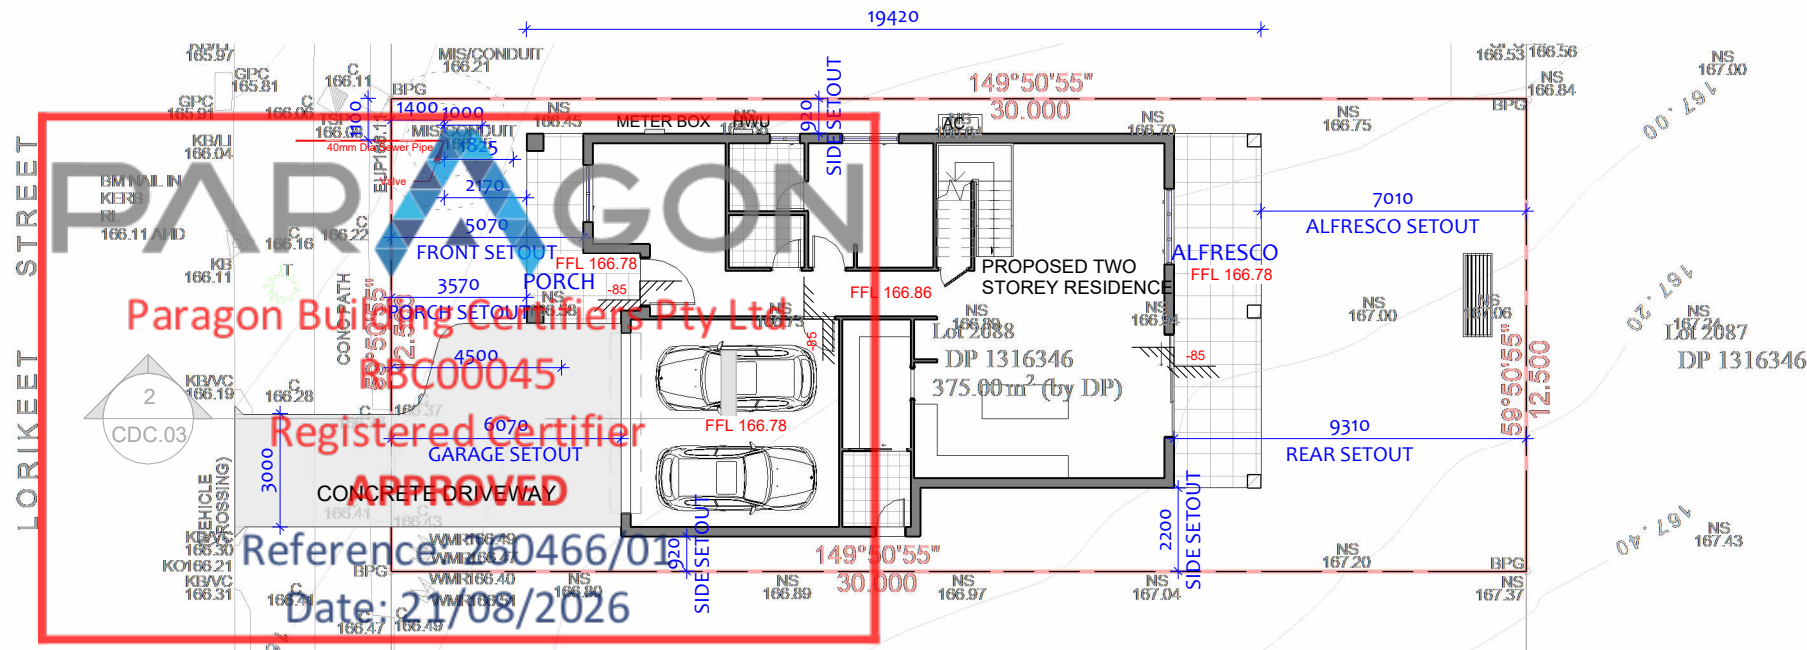

1 CDC - SITE PLAN
1 : 200

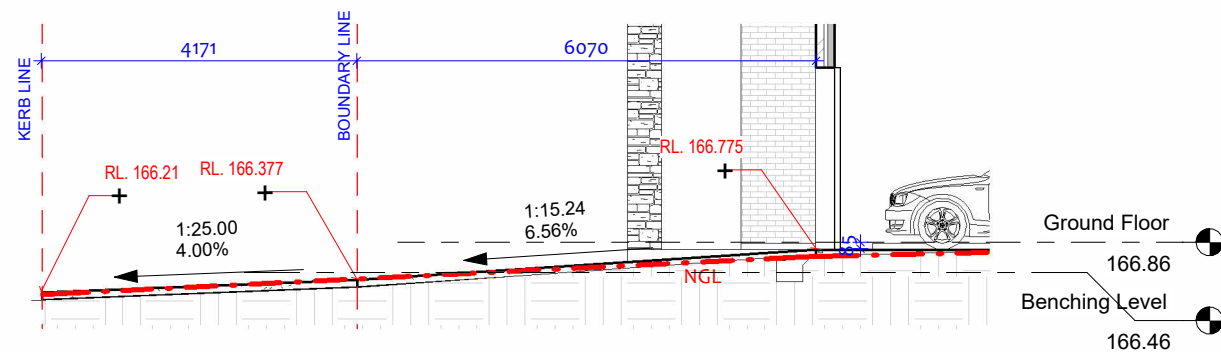

2 DRIVEWAY SECTION
1 : 100

AREA SCHEDULE (RENTABLE)	
NAME	AREA (m2)
LOT AREA	375
GROUND FLOOR	106
FIRST FLOOR	122
GARAGE	30
STAIRSCASE VOID	6
PRIVATE OPEN SPACE	24
DRIVEWAY	28
FRONT LANDSCAPE	22.7
REAR LANDSCAPE	113.35

WILTON GREENFIELD HOUSING CODE COMPLIANCE TABLE

DESCRIPTION		COMPLIANCE		COMMENT
ELEMENT	CODE CONTROL	REQUIREMNT	PROPOSED	
LOAND ZONE	1 GENERAL RESIDENTIAL			
LOT NO	LOT 2088			
LOT AREA	375.00 m2			
LOT WIDTH	Standard Lot Min. 8m at Building Line facing primary road	8.0m	12.5 m	YES
HEIGHT	MAX. Height	8.5m	8.3m (MAX.)	YES
FRONT SETBACK	FRONT SET BACK (Min. Setback from Primary Road) For 300-350 sqm. Lot	4.5 m	4.5m	YES
REAR SET BACK (MIN.)	GROUND FLOOR	4.5m	9.8m	YES
	FIRST FLOOR	6m	9.8m	
SIDE SET BACK (MIN.)	GROUND FLOOR	0/0.9m	0.9/0.9m	YES
	FIRST FLOOR	1.5/0.9m	2.2/0.9m	
FLOOR SPACE RATIO (FSR)	25% Lot area + 150m2	243.75m2	240 m2	YES
GROSS FLOOR AREA PLAN	GROUND FLOOR		106 m2	
	FIRST FLOOR		122 m2	
TOTAL FLOOR AREA			228 m2	
ROOF AREA			235 m2	
GARAGE			30 m2	
PRIVATE OPEN SPACE	>10m Lot width	24m2	24 m2	YES
LANDSCAPE AREA	20 % of TOTAL LAND AREA	75 m2	136.05 m2	YES

REV	DATE	DESCRIPTION	BY
6	15-07-2026	Porch and balcony Extended to 1500mm, balcony above garage reduce to 1500mm, Cladding return on Balcony, Gable Roof on Facade as per developer, All Electric cooktop and Solar added. Area increase to 237 sq.m - Ekta/Developer	
5	25-06-2026	CDC ISSUE	



RUBY HOMES

THIS DRAWING IS THE EXCLUSIVE PROPERTY OF THE DEVELOPER & THE REPRODUCTION OF ANY PART WITHOUT THE PRIOR WRITTEN CONSENT OF THE DEVELOPER IS A VIOLATION OF APPLICABLE LAWS. IN NO EVENT SHALL THE DEVELOPER BE HELD LIABLE FOR SPECIAL COLLATERAL, INCIDENTAL OR CONSEQUENTIAL LIABILITY IN CONNECTION WITH THE USE OF THIS DIGITAL DATA ONCE RELEASED FROM THE DEVELOPER'S OFFICE. THIS DRAWING IS TO BE READ & UNDERSTOOD IN CONJUNCTION WITH THE STRUCTURAL, MECHANICAL, ELECTRICAL & / OR ANY OTHER CONSULTANT'S DOCUMENTATION AS MAY BE APPLICABLE TO THE PROJECT PRIOR TO THE START OF ANY WORKS AND FOR ITS DURATION.

PROJECT:
Lot 2088 13 LORIKEET STREET
13 LORIKEET STREET WILTON

DRAWING TITLE:
LOCATION PLAN AND SITE PLAN



LOT NO: 2088	DATE: 20-08-2026	SCALE: As indicated	DRAWING No: CDC.03	REV: 6
DRAWN BY: AS	CHECKED BY: RH			ISSUED BY:
DRAFTED BY: SL	CLIENT NAME: Bhasker Maskey & Sabnam Karki			

CDC ISSUE

LORIKEET STREET



TEMPORARY 1.8M HIGH WIRE ML FENCE WITH DUSTPROOF MESH APPLIED TO FULL HEIGHT TO BOUNDARIES AS REQUIRED

LOCATION OF WASTE BINS
SEDIMENT FENCE AS REQUIRED
GRAVEL ACCESS
SITE ACCESS AREA TO BE USED FOR WASHDOWN AREA
FOOTPATH CLEAN AND CLEAR AT ALL TIMES

LOCATION OF STOCKPILE MATERIAL
MATERIAL STORAGE AREA
TEMPORARY TOILETS
INSTALL TEMPORARY SEDIMENT BARRIERS TO ALL INLET PITS LIKELY TO COLLECT SILT LADEN WATER, TO COUNCIL'S REQUIREMENTS.

SEDIMENT AND EROSION NOTES:

- THIS PLAN TO BE READ IN CONJUNCTION WITH SEDIMENT AND EROSION CONTROL DETAILS AS ATTACHED.
- THE CONTRACTOR SHALL IMPLEMENT ALL SOIL EROSION AND SEDIMENT CONTROL MEASURES AS NECESSARY AND TO THE SATISFACTION OF COUNCIL PRIOR TO THE COMMENCEMENT AND DURING CONSTRUCTION. NO DISTURBANCE TO THE SITE SHALL BE PERMITTED OTHER THAN IN THE IMMEDIATE AREA OF THE WORK AND NO MATERIAL SHALL BE REMOVED FROM THE SITE WITHOUT COUNCIL'S APPROVAL. ALL SEDIMENT AND EROSION CONTROL DEVICES TO BE INSTALLED AND MAINTAINED IN ACCORDANCE WITH STANDARDS OUTLINED IN NSW DEPARTMENT OF HOUSING "MANAGING URBAN STORMWATER-SOILS AND CONSTRUCTIONS".
- TOPSOIL SHALL BE STRIPPED AND STOCKPILED OUTSIDE HAZARD AREAS SUCH AS DRAINAGE LINES. THIS TOP SOIL IS TO BE RESPIRED LATER ON AREAS TO BE REVEGETATED AND STABILISED ONLY. (I.E ALL FOOTPATHS, BATTERS, SITE REGARDING AREAS, BASINS AND CATCH DRAINS), TOPSOIL SHALL NOT BE RESPIRED ON ANY OTHER AREAS UNLESS SPECIALLY INSTRUCTED BY THE SUPERIDENT. IF THEY ARE TO REMAIN FOR LONGER THAN ONE MONTH STOCKPILES SHALL BE PROTECTED FROM EROSION BY COVERING THEM WITH A MULCH AND HYDROSEEDING AND, IF NECESSARY, BY LOCATING BANKS OR DRAINS DOWNSTREAM OF A STOCKPILE TO RETARD SILT LADEN RUNOFF.
- THE CONTRACTOR SHALL REGULARLY MAINTAIN ALL SEDIMENT AND EROSION CONTROL DEVICES AND REMOVE ACCUMULATED SILT FROM SUCH DEVICES SUCH THAT MORE THAN 60% OF THEIR CAPACITY LOST. ALL THE SILTS TO BE PLACED OUTSIDE THE LIMIT OF WORKS. THE PERIOD FOR MAINTAINING THESE DEVICES SHALL BE AT LEAST UNTIL ALL DISTURBED AREAS ARE REVEGETATED AND FURTHER AS MAY BE DIRECTED BY THE SUPERINTENDENT OR COUNCIL.
- LAY TURF STRIP (MIN 300 mm WIDE) ON 100 mm TOPSOIL WITH 1.0 m LONG RETURNS EVERY 6.0m BEHIND ALL KERB AT THE TOP OF ALL BATTERS AND AROUND STRUCTURES IMMEDIATELY AFTER BACKFILLING OR FORMATION.
- THE CONTRACTOR SHALL GRASS SEED ALL DISTURBED AREAS WITH AN APPROVED MIX AS SSON AS PRACTICABLE AFTER COMPLETION OF EARTHWORKS AND REGRADING.
- VEHICULAR TRAFFIC SHALL BE CONTROLLED DURING CONSTRUCTION CONFINING ACCESS WHERE POSSIBLE TO NOMINATED STABILISED ACCESS POINTS.
- WHEN ANY DEVICES ARE TO BE HANDED OVER TO COUNCIL, THEY SHALL BE IN CLEAN AND STABLE CONDITION.
- THE CONTRACTOR SHALL IMPLEMENT DUST CONTROL BY REGULAR WETTING DOWN (BUT NOT SATURATING) DISTURBED AREA.
- PROVIDE AND MAINTAIN SILT TRAPS AROUND ALL SURFACE INLET PITS UNTIL CATCHMENT IS REVEGETATED OR PAVED.
- REVEGETATE ALL TRENCHES IMMEDIATELY UPON COMPLETION OF BACKFILLING.
- ALL DRAINAGE PIPE INLETS TO BE CAPPED UNTIL:
 - DOWNPINES CONNECTED
 - PITS CONSTRUCTED & PROTECTED WITH SILT

CDC - SITE ANALYSIS AND SEDIMENT CONTROL PLAN

1 : 200

SD 6-9 GEOTEXTILE INLET FILTER





- FABRICATE A SEDIMENT BARRIER MADE FROM GEOTEXTILE. REFER SD6-7 FOR DETAILS.
- SUPPORT GEOTEXTILE WITH MESH TIED TO POSTS AT 1 m Ctrs.
- DO NOT COVER INLET WITH GEOTEXTILE.

SITE WORKS NOTES

- ORIGIN OF LEVELS PROVIDED BY SURVEYOR
- THE BUILDER SHALL VERIFY ALL DIMENSIONS AND EXISTING LEVELS ON SITE PRIOR TO THE COMMENCEMENT OF WORK AND ANY DISCREPANCIES SHALL BE REPORTED TO THE SURVEYOR / ENGINEER.
- TOPSOIL SHALL BE STRIPPED FROM THE CONSTRUCTION AREA AND STOCKPILED ON SITE, TO BE LATER SPREAD OR DISPOSED OFF SITE AS DIRECTED BY SUPERVISOR / ENGINEER.
- ALL TRENCH BACKFILL MATERIAL SHALL BE COMPACTED TO THE SAME DENSITY AS THE ADJACENT MATERIAL.
- ALL SERVICE TRENCHES UNDER VEHICULAR PAVEMENTS SHALL BE BACKFILLED WITH SAND OR APPROVED GRANULAR MATERIALS. TO THE UNDERSIDE OF THE PAVEMENT, AND COMPACTED TO 98% STANDARD MAXIMUM DRY DENSITY, IN ACCORDANCE WITH AS 1289E1.1.

SD 5-7 STABILISED SITE ACCESS

- STRIP TOPSOIL AND LEVEL SITE.
- COMPACT SUBGRADE.
- COVER AREA WITH GEOTEXTILE.
- CONSTRUCT 200 mm THICK PAD OVER GEOTEXTILE USING ROADBASE OR 30 mm AGGREGATE. Min 15 m LONG OR TO BUILDING ALIGNMENT. Min 3 m WIDE.
- CONSTRUCT HUMP IMMEDIATELY WITHIN BOUNDARY TO DIVERT WATER TO A SEDIMENT FENCE OR OTHER SEDIMENT TRAP.

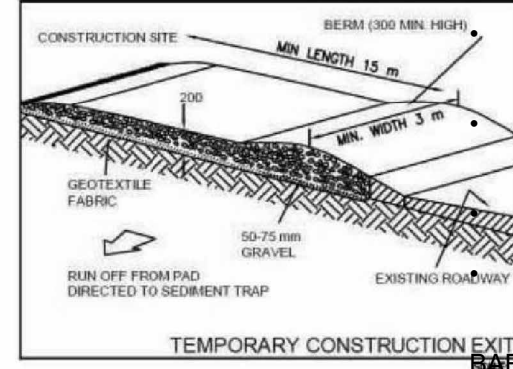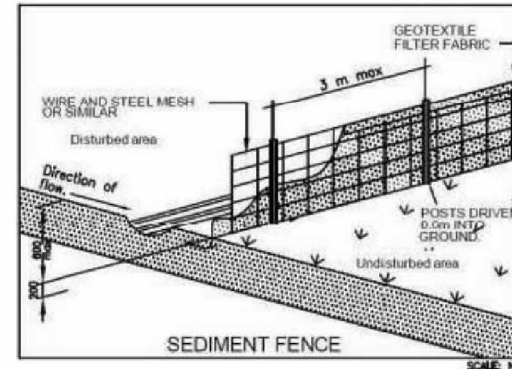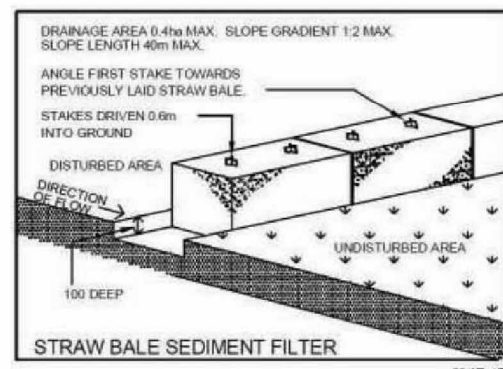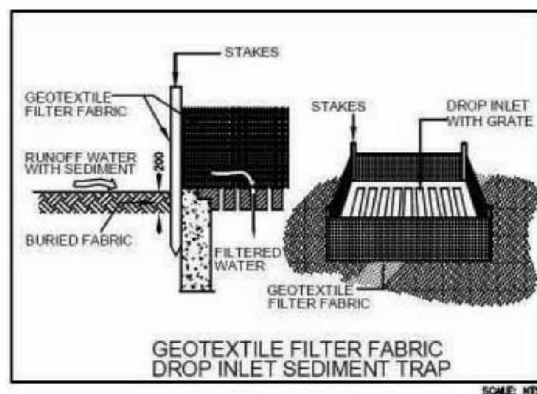


REV	DATE	DESCRIPTION	BY
6	15-07-2026	Porch and balcony Extended to 1500mm, balcony above garage reduce to 1500mm, Cladding return on Balcony, Gable Roof on Facade as per developer, All Electric cooktop and Solar added. Area increase to 237 sq.m - Ekta/Developer	
5	25-06-2026	CDC ISSUE	

RUBY HOMES

THIS DRAWING IS THE EXCLUSIVE PROPERTY OF THE DEVELOPER & THE REPRODUCTION OF ANY PART WITHOUT THE PRIOR WRITTEN CONSENT OF THE DEVELOPER IS A VIOLATION OF APPLICABLE LAWS. IN NO EVENT SHALL THE DEVELOPER BE HELD LIABLE FOR SPECIAL COLLATERAL, INCIDENTAL OR CONSEQUENTIAL LIABILITY IN CONNECTION WITH THE USE OF THIS DIGITAL DATA ONCE RELEASED FROM THE DEVELOPER'S OFFICE. THIS DRAWING IS TO BE READ & UNDERSTOOD IN CONJUNCTION WITH THE STRUCTURAL, MECHANICAL, ELECTRICAL & / OR ANY OTHER CONSULTANT'S DOCUMENTATION AS MAY BE APPLICABLE TO THE PROJECT PRIOR TO THE START OF ANY WORKS AND FOR ITS DURATION.

PROJECT:
Lot 2088 13 LORIKEET STREET
13 LORIKEET STREET WILTON

DRAWING TITLE:
SITE ANALYSIS AND SEDIMENT CONTROL

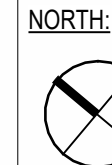


LOT NO:	DATE:	SCALE:	DRAWING No:	REV:
2088	20-08-2026	As indicated	CDC.04	6
DRAWN BY:	CHECKED BY:	DRAFTED BY:	CLIENT NAME:	ISSUED BY:
AS	RH	SL	Bhasker Maskey & Sabnam Karki	

CDC ISSUE

☑ BAL – LOW


IMPORTANT NOTES:
ALL DIMENSIONS AND NOTES ON ALL PLANS MUST BE CHECKED AND VERIFIED BY BUILDERS AND OWNER PRIOR TO COMMENCEMENT OF ANY BUILDING WORKS. TO CLARIFY AND CONFIRM WITH CONSTRUCTION COMPANY FOR DISCREPANCIES ON ALL DOCUMENTS AND PLANS PROVIDED FOR CONSTRUCTION. ANY WORK INDICATED ON THE PLAN BUT NOT IN THE SPECIFICATION BUT WHICH IS NECESSARY AS PART OF THE CONTRACT, VARIATION TO PLANS, SPECIFICATIONS MAY NOT BE MADE WITHOUT THE WRITTEN CONSENT OF OWNER. IT IS THE RESPONSIBILITY OF THE BUILDER/END USER TO VERIFY PLANS AND SPECIFICATIONS AS TO THEIR ACCURACY AND COMPLY CURRENT BCA AND AUSTRALIAN STANDARDS. WINDOWS TO COMPLY WITH 3.9.3.5 OF THE BCA.

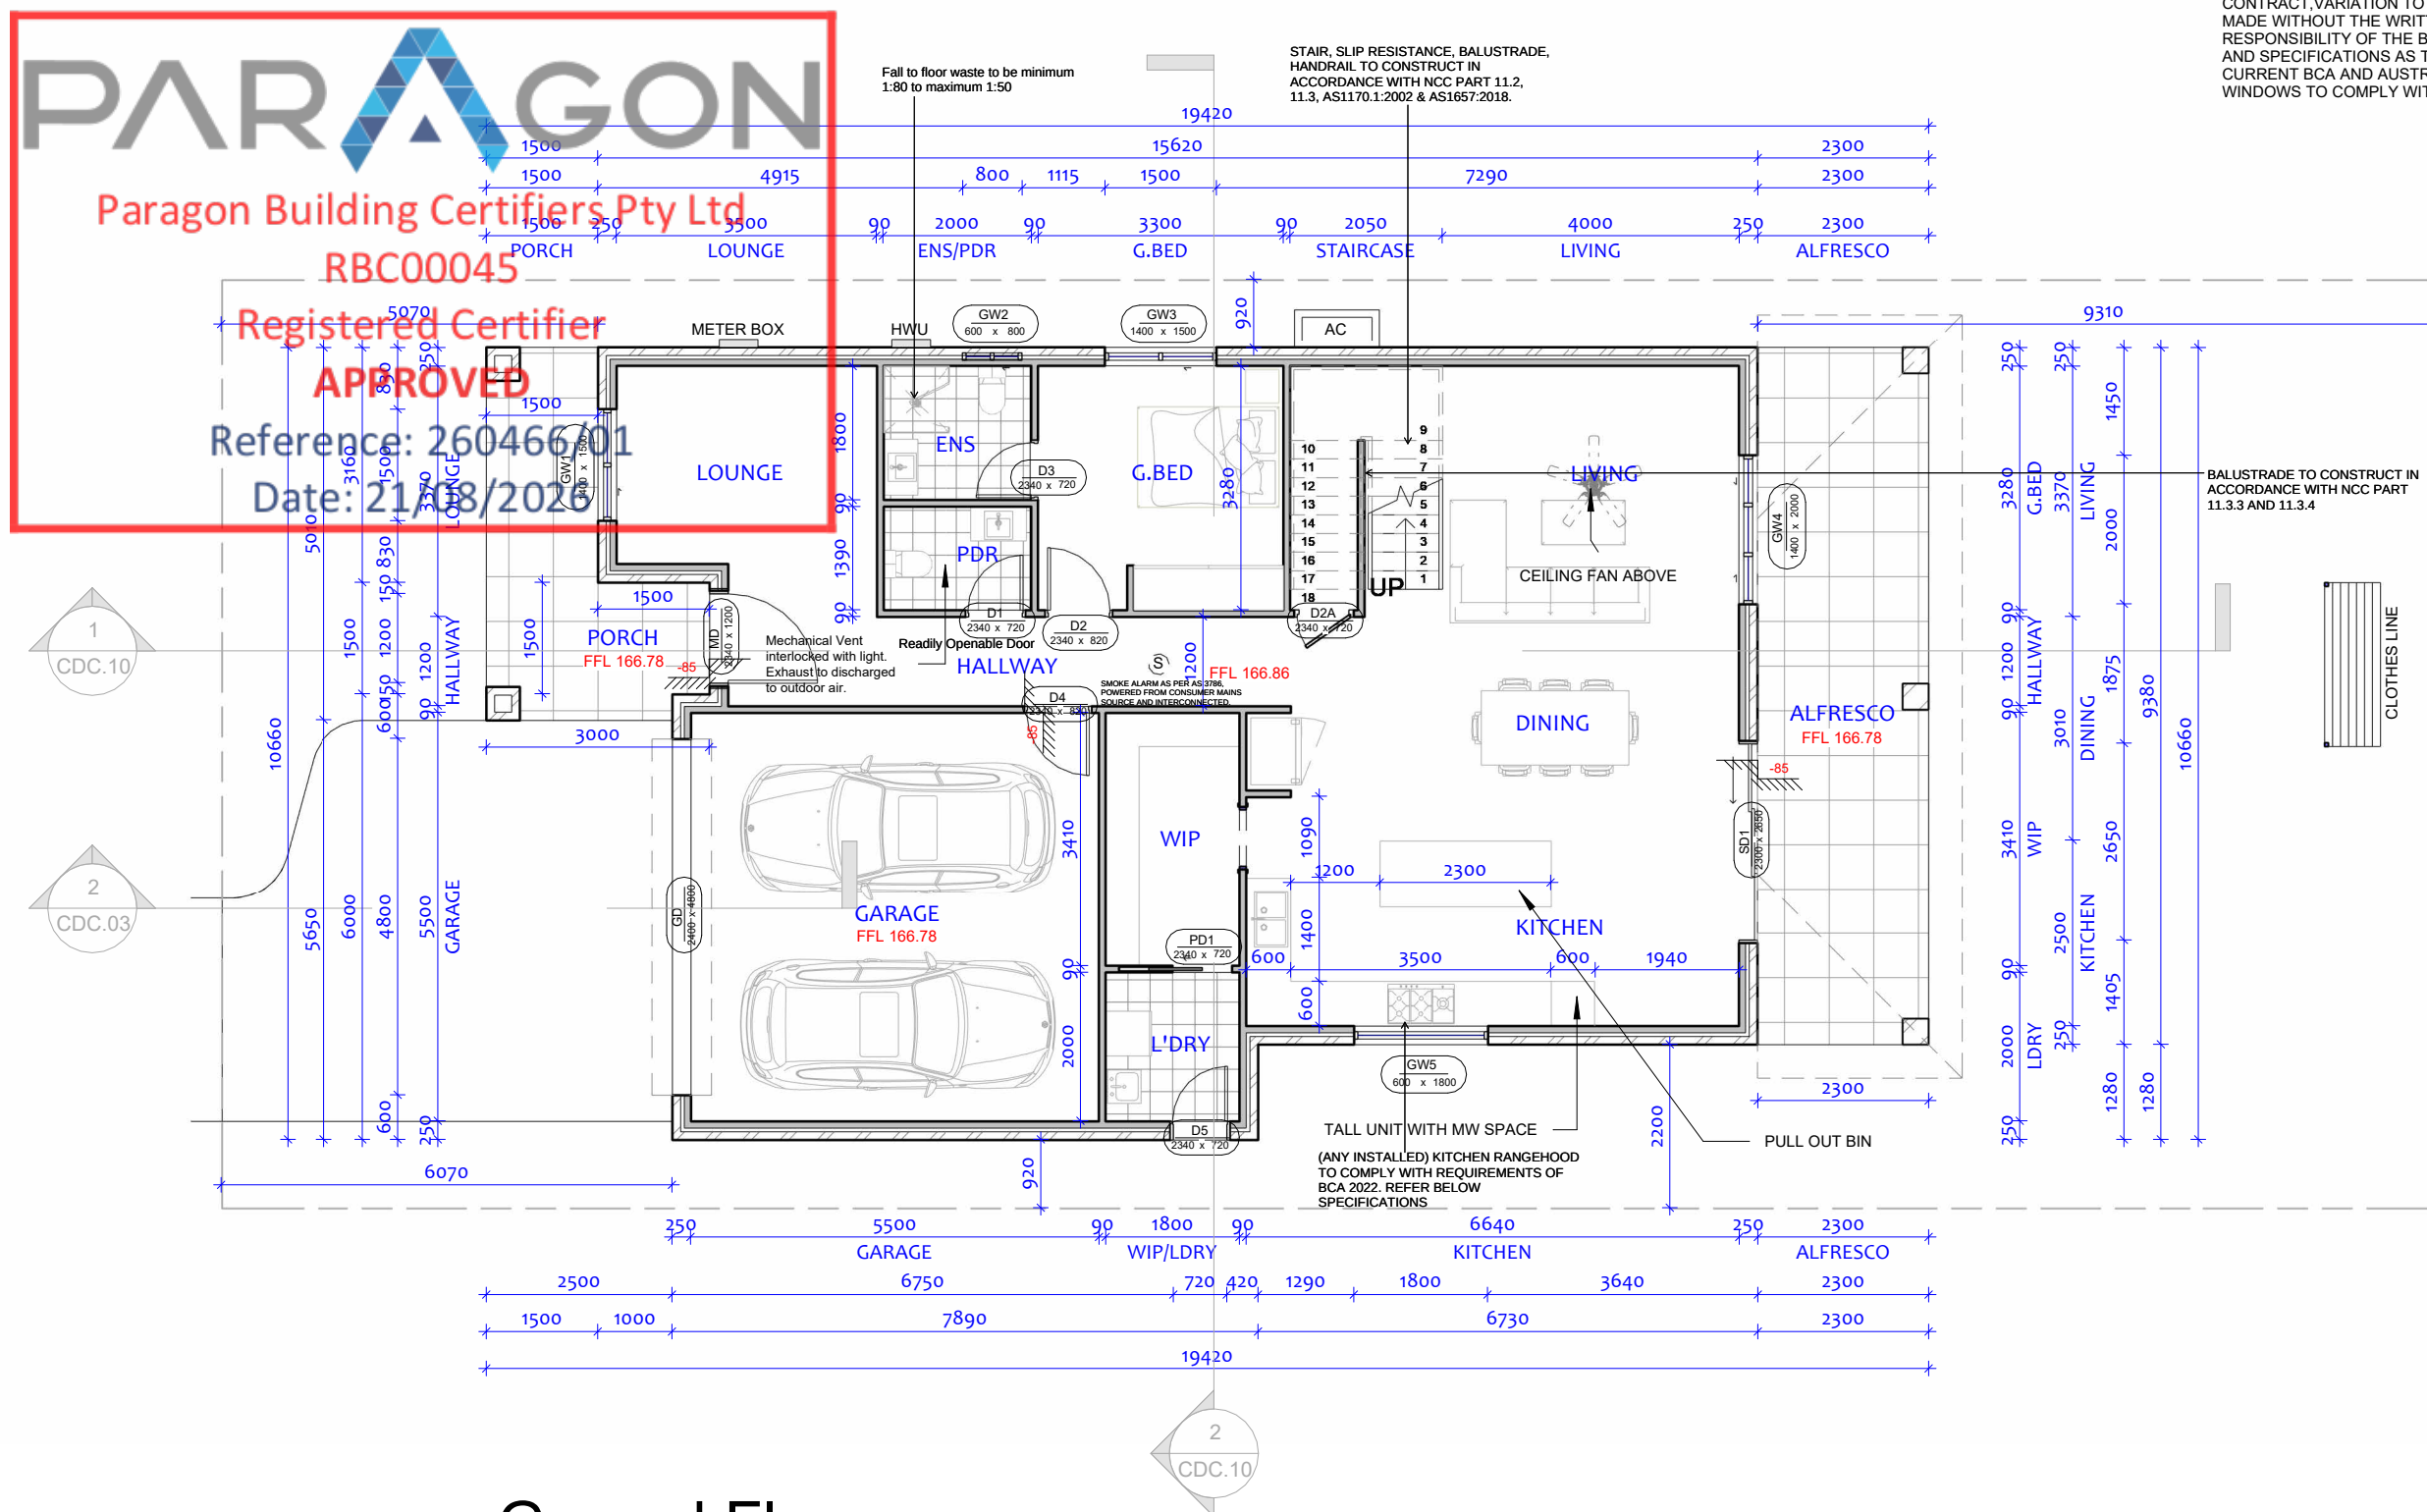

NOTE: PLEASE REFER TO TENDER FOR ALL INCLUSIONS.


Connection to a recycled water reticulation system for all non-potable use

REV	DATE	DESCRIPTION	BY
11	Date 11	Glass railing at balcony, LP gas - Ekta/Client	
8	27-07-2026	Facade Updated with stone and wooden cladding - Bishwas/Sheela	
6	15-07-2026	Porch and balcony Extended to 1500mm, balcony above garage reduce to 1500mm, Cladding return on Balcony, Gable Roof on Facade as per developer, All Electric cooktop and Solar added. Area increase to 237 sq.m - Ekta/Developer	
5	25-06-2026	CDC ISSUE	

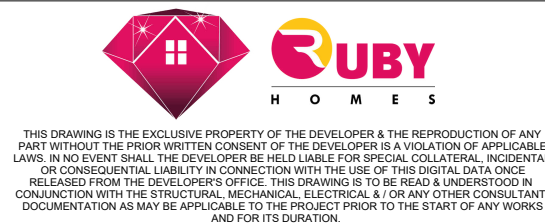

PROJECT:
Lot 2088 13 LORIKEET STREET
13 LORIKEET STREET WILTON

DRAWING TITLE:
GROUND FLOOR PLAN

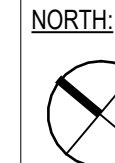


LOT NO:	DATE:	SCALE:	DRAWING No:	REV:
2088	20-08-2026	1 : 100	CDC.05	11
DRAWN BY:	CHECKED BY:			ISSUED BY:
AS	RH			
DRAFTED BY:	CLIENT NAME:			
SL	Bhasker Maskey & Sabnam Karki			

CDC ISSUE

☒ BAL – LOW


IMPORTANT NOTES:
ALL DIMENSIONS AND NOTES ON ALL PLANS MUST BE CHECKED AND VERIFIED BY BUILDERS AND OWNER PRIOR TO COMMENCEMENT OF ANY BUILDING WORKS. TO CLARIFY AND CONFIRM WITH CONSTRUCTION COMPANY FOR DISCREPANCIES ON ALL DOCUMENTS AND PLANS PROVIDED FOR CONSTRUCTION. ANY WORK INDICATED ON THE PLAN BUT NOT IN THE SPECIFICATION BUT WHICH IS NECESSARY AS PART OF THE CONTRACT, VARIATION TO PLANS, SPECIFICATIONS MAY NOT BE MADE WITHOUT THE WRITTEN CONSENT OF OWNER. IT IS THE RESPONSIBILITY OF THE BUILDER/END USER TO VERIFY PLANS AND SPECIFICATIONS AS TO THEIR ACCURACY AND COMPLY CURRENT BCA AND AUSTRALIAN STANDARDS. WINDOWS TO COMPLY WITH 3.9.3.5 OF THE BCA.

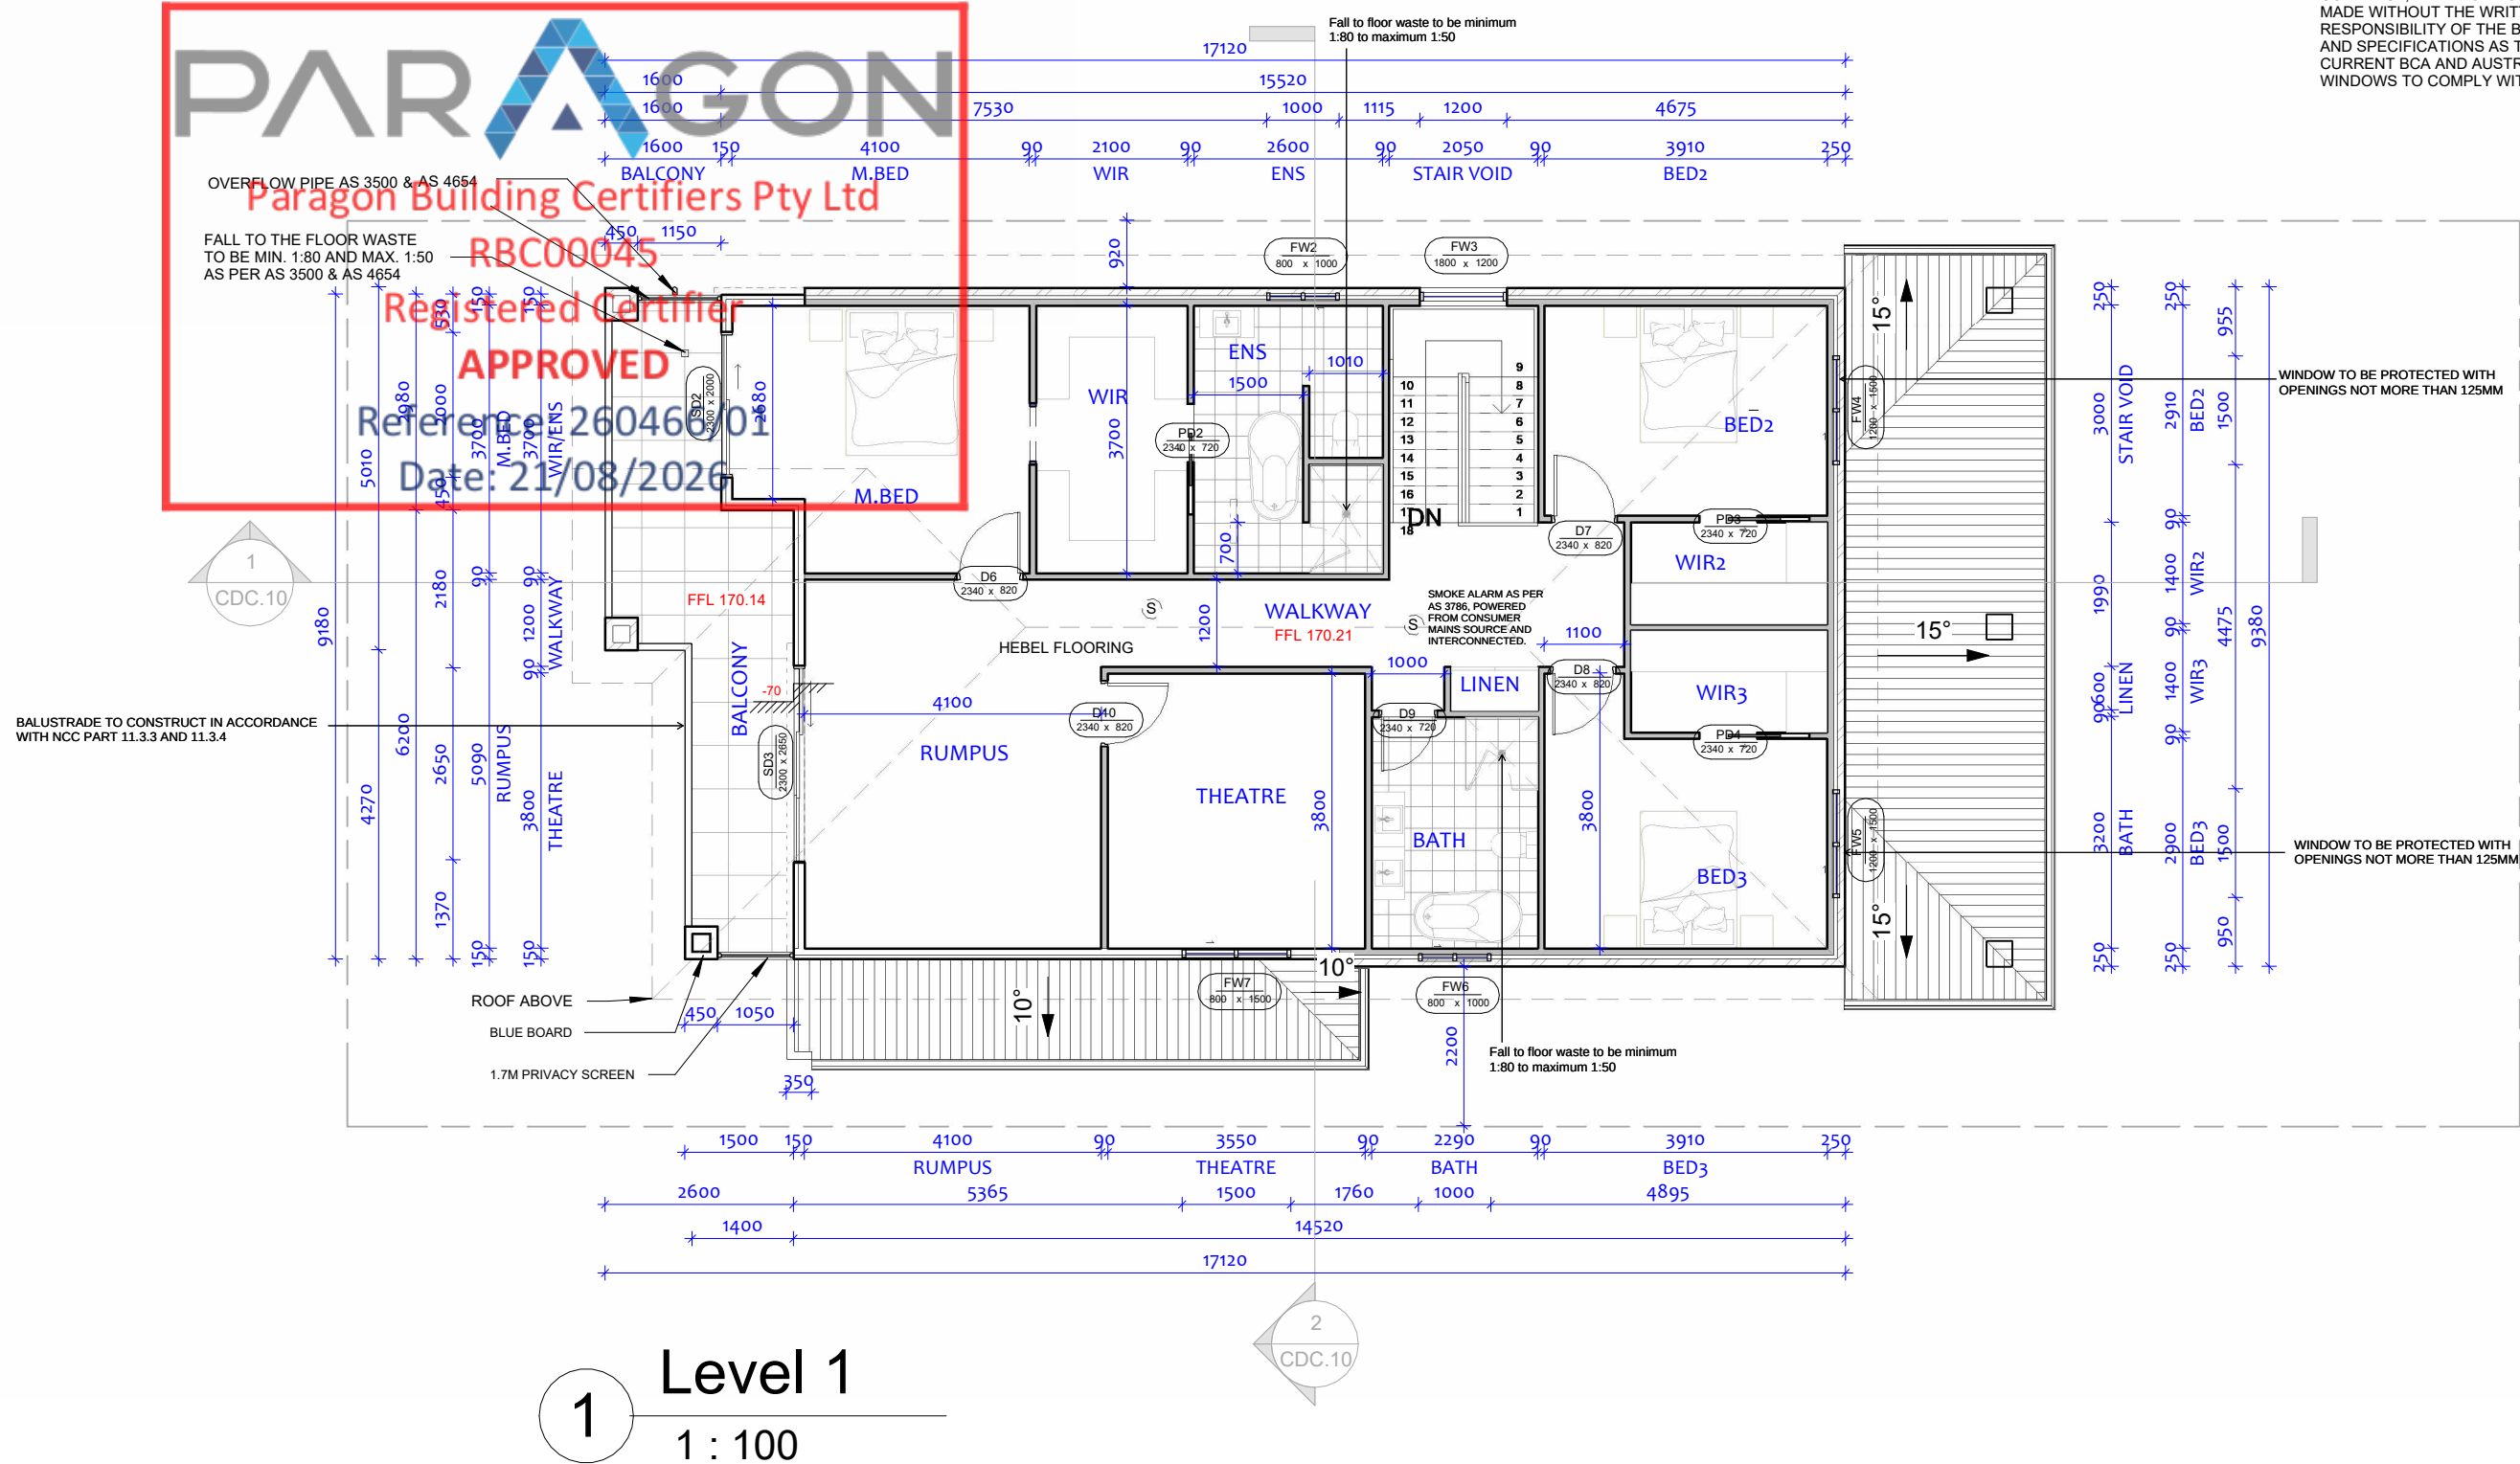

NOTE: PLEASE REFER TO TENDER FOR ALL INCLUSIONS.


Connection to a recycled water reticulation system for all non-potable use

REV	DATE	DESCRIPTION	BY
11	Date 11	Glass railing at balcony, LP gas - Ekta/Client	
10	30-07-2026	Metal Railing on Balcony - Developer/Client	
9	28-07-2026	Full Cladding on Front facade on first floor - Bishwas	
8	27-07-2026	Facade Updated with stone and wooden cladding - Bishwas/Sheela	
7	16-07-2026	Metal Railings on balcony - Ekta	

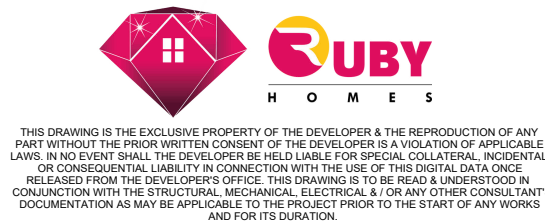

PROJECT:
Lot 2088 13 LORIKEET STREET
13 LORIKEET STREET WILTON

DRAWING TITLE:
FIRST FLOOR LEVEL

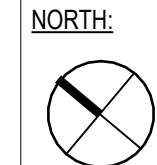

LOT NO:	DATE:	SCALE:	DRAWING No:	REV:
2088	20-08-2026	1 : 100	CDC.06	11
DRAWN BY:	CHECKED BY:			ISSUED BY:
AS	RH			
DRAFTED BY:	CLIENT NAME:			
SL	Bhasker Maskey & Sabnam Karki			

CDC ISSUE

☒ BAL – LOW

IMPORTANT NOTES:
ALL DIMENSIONS AND NOTES ON ALL PLANS MUST BE CHECKED AND VERIFIED BY BUILDERS AND OWNER PRIOR TO COMMENCEMENT OF ANY BUILDING WORKS. TO CLARIFY AND CONFIRM WITH CONSTRUCTION COMPANY FOR DISCREPANCIES ON ALL DOCUMENTS AND PLANS PROVIDED FOR CONSTRUCTION. ANY WORK INDICATED ON THE PLAN BUT NOT IN THE SPECIFICATION BUT WHICH IS NECESSARY AS PART OF THE CONTRACT, VARIATION TO PLANS, SPECIFICATIONS MAY NOT BE MADE WITHOUT THE WRITTEN CONSENT OF OWNER. IT IS THE RESPONSIBILITY OF THE BUILDER/END USER TO VERIFY PLANS AND SPECIFICATIONS AS TO THEIR ACCURACY AND COMPLY CURRENT BCA AND AUSTRALIAN STANDARDS. WINDOWS TO COMPLY WITH 3.9.3.5 OF THE BCA.

ABCB HOUSING PROVISIONS STANDARD 2022

10.8.3 VENTILATION OF ROOF SPACES

1. IN CLIMATE ZONES 6,7 AND 8, A ROOF MUST HAVE A ROOF SPACE THAT


(A) IS LOCATED

- (I) IMMEDIATELY ABOVE THE *PRIMARY INSULATION LAYER*, OR
(II) IMMEDIATELY ABOVE SARKING WITH A *VAPOUR PERMEANCE* OF NOT LESS THAN 1.14 µG/N.S, WHICH IS IMMEDIATELY ABOVE THE *PRIMARY INSULATION LAYER* OR
(III) IMMEDIATELY ABOVE CEILING INSULATION THAT MEETS THE REQUIREMENTS OF 13.2.3(3) AND 13.2.3(4); AND

(B) HAS A HEIGHT OF NOT LESS THAN 20MM; AND

(C) IS EITHER -

- (I) VENTILATED TO OUTDOOR AIR THROUGH EVENLY DISTRIBUTED OPENINGS IN ACCORDANCE WITH TABLE 10.8.3; OR
(II) LOCATED IMMEDIATELY UNDERNEATH THE ROOF TILES OF A UNSARKED TILED ROOF.

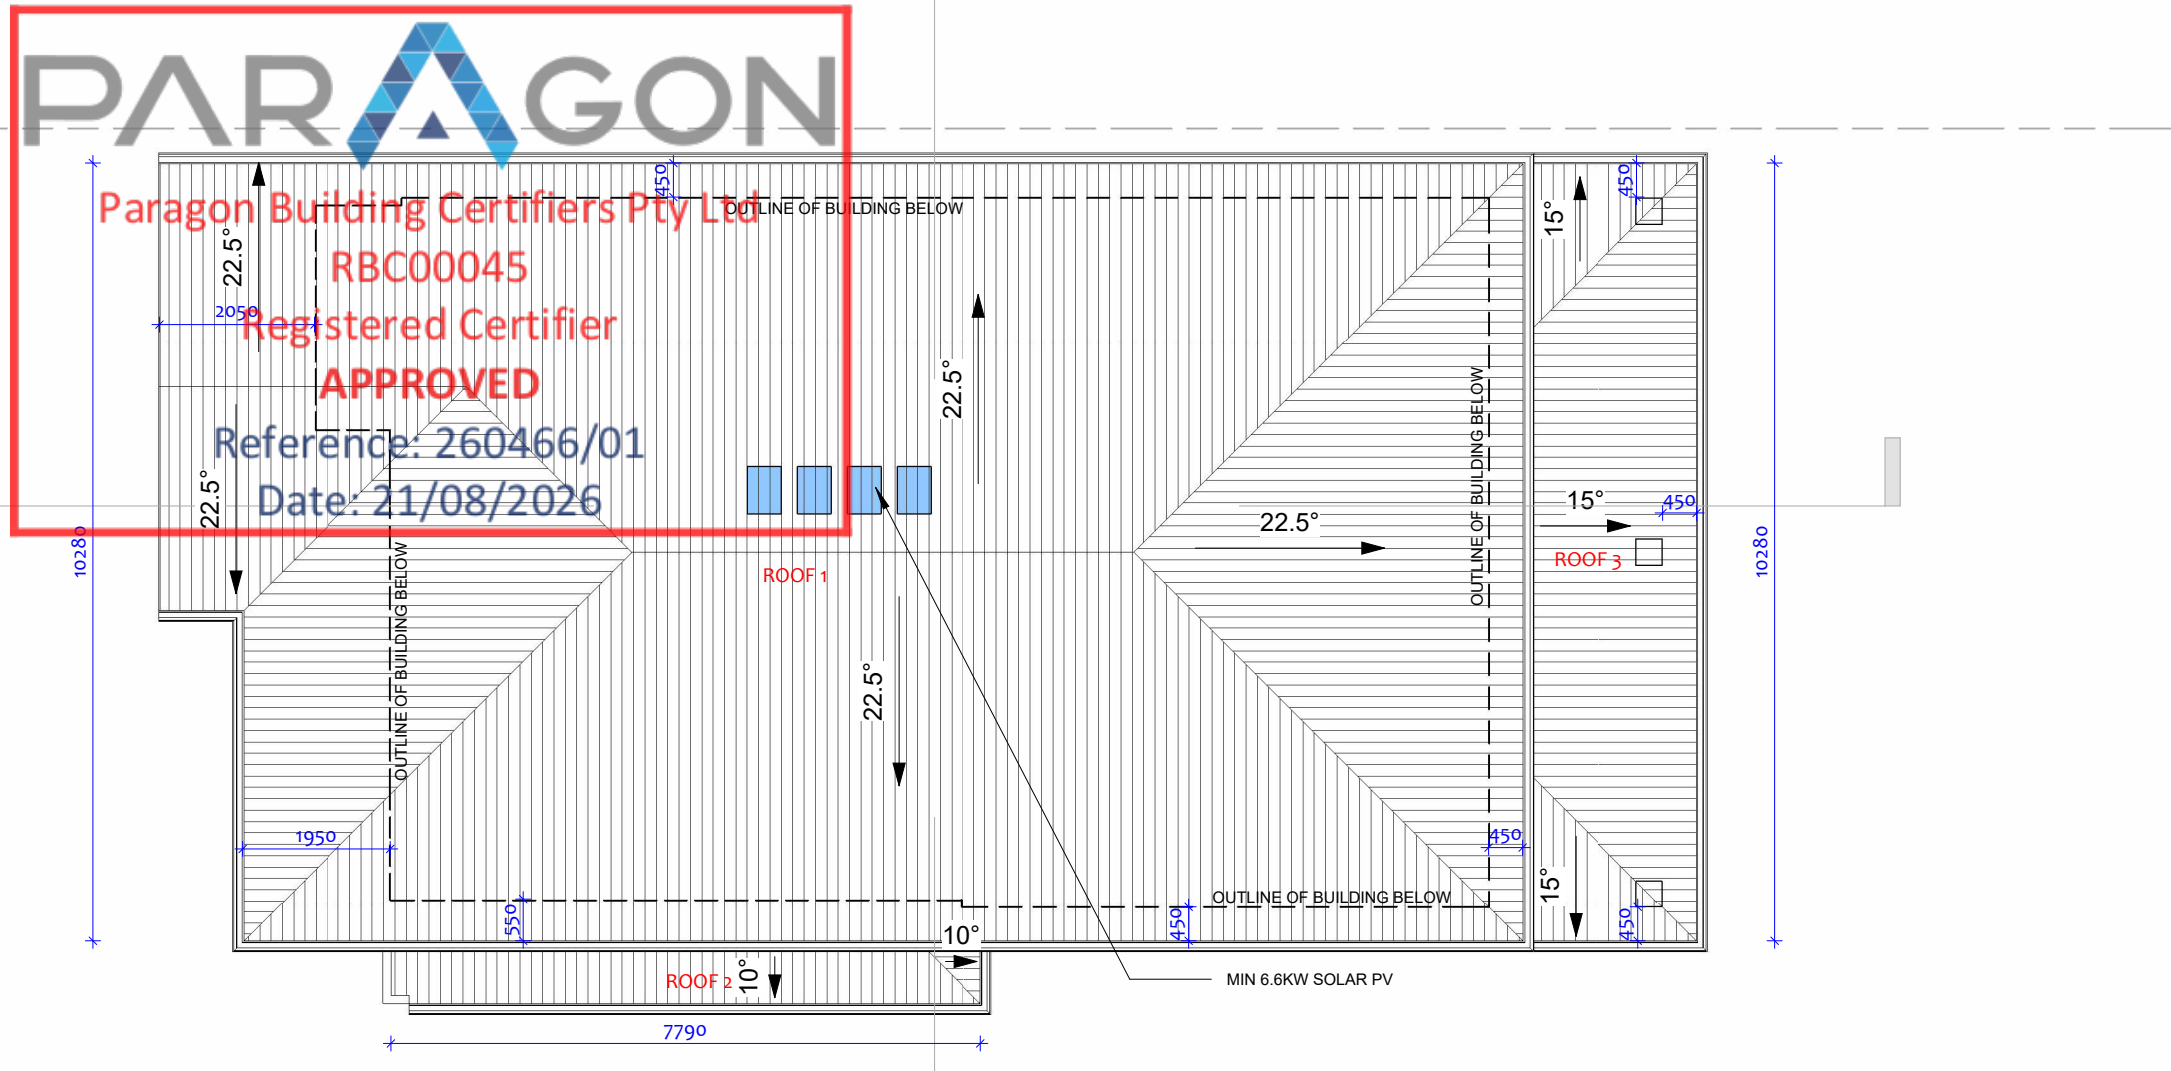

1 ROOF PLAN

1 : 100

Figure 7.2.3: Minimum pitch requirements for metal roofing profiles

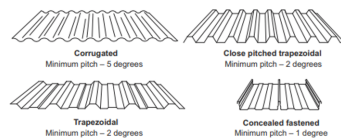


Table 10.8.3: Roof space ventilation requirements

Roof pitch	Ventilation openings
< 10°	25,000 mm ² /m provided at each of two opposing ends
≥ 10° and < 15°	25,000 mm ² /m provided at the eaves and 5,000 mm ² /m at high level
≥ 15° and < 75°	7,000 mm ² /m provided at the eaves and 5,000 mm ² /m at high level, plus an additional 18,000 mm ² /m at the eaves if the roof has a cathedral ceiling

Figure 10.8.3 (explanatory): Example of roof space with low level ventilation

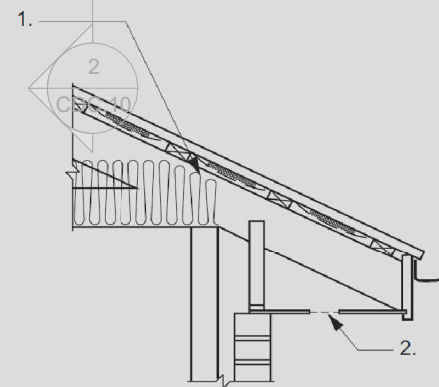


Figure Notes

- (1) Minimum 20 mm gap maintained between insulation and sarking.
(2) Eave ventilation opening in accordance with Table 10.8.3.

Roof Schedule


Mark	Base Level	Area	Comments
------	------------	------	----------

ROOF1	CEILING LEVEL	195 m ²	COLORBOND(0.7 SA)
ROOF3	Level 1	29 m ²	COLORBOND(0.7 SA)
ROOF2	Level 1	11 m ²	COLORBOND(0.7 SA)

Grand total: 3 235 m²


CDC ISSUE

REV	DATE	DESCRIPTION	BY
8	27-07-2026	Facade Updated with stone and wooden cladding - Bishwas/Sheela	
6	15-07-2026	Porch and balcony Extended to 1500mm, balcony above garage reduce to 1500mm, Cladding return on Balcony, Gable Roof on Facade as per developer, All Electric cooktop and Solar added. Area increase to 237 sq.m - Ekta/Developer	
5	25-06-2026	CDC ISSUE	


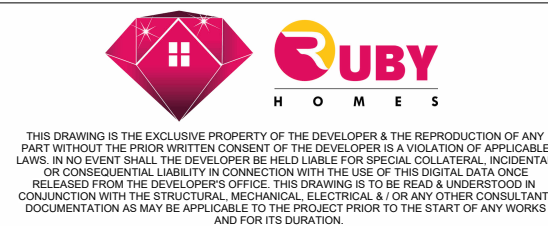


PROJECT:
Lot 2088 13 LORIKEET STREET
13 LORIKEET STREET WILTON

DRAWING TITLE:
ROOF PLAN

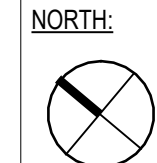

LOT NO:	DATE:	SCALE:	DRAWING No:	REV:
2088	20-08-2026	1 : 100	CDC.07	8
DRAWN BY:	CHECKED BY:			ISSUED BY:
AS	RH			
DRAFTED BY:	CLIENT NAME:			
SL	Bhasker Maskey & Sabnam Karki			

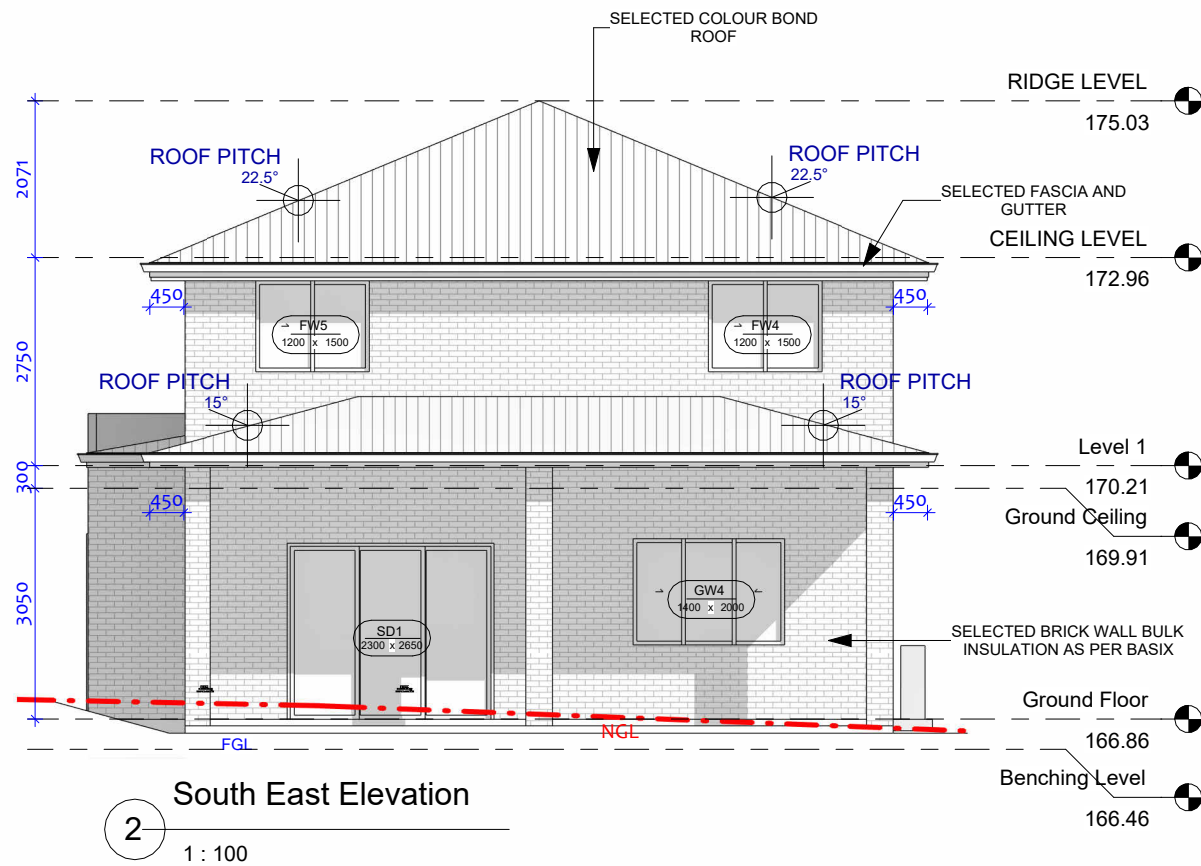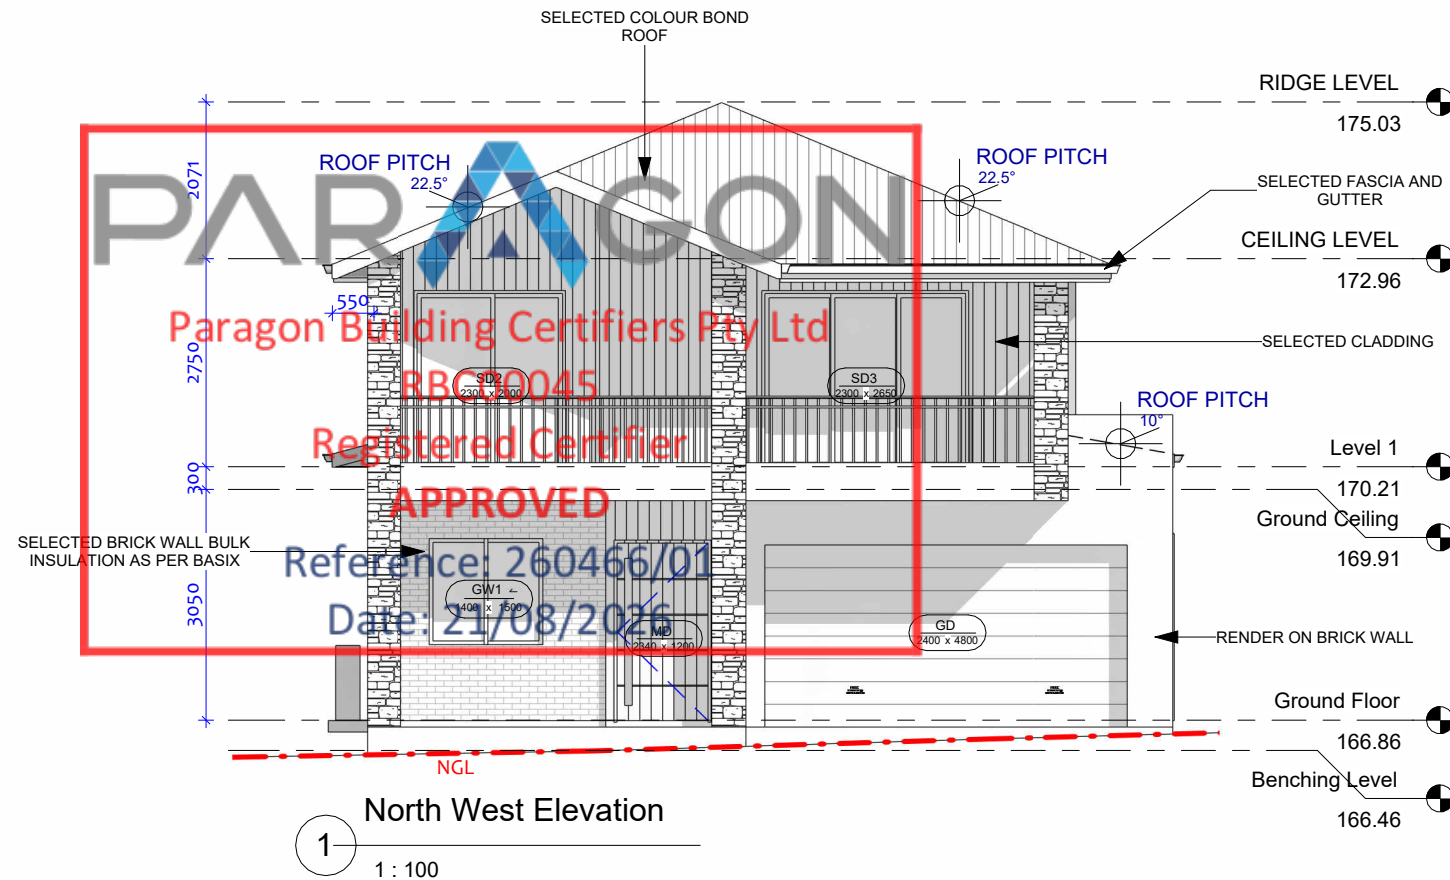

Window Schedule 1

Mark	Height	Width	Sill Height	Head Height	Description
Ground Floor					
GW1	1400	1500	1000	2400	SLIDING
GW2	600	800	1800	2400	SLIDING
GW3	1400	1500	1000	2400	SLIDING
GW4	1400	2000	1000	2400	SLIDING & FIXED
GW5	600	1800	1000	1600	FIXED

Ground Floor: 5

Level 1

FW2	800	1000	1650	2450	SLIDING
FW3	1800	1200	650	2450	FIXED
FW4	1200	1500	1250	2450	SLIDING
FW5	1200	1500	1250	2450	SLIDING
FW6	800	1000	1650	2450	SLIDING
FW7	800	1500	1650	2450	SLIDING

Level 1: 6

Door Schedule 1

Mark	Height	Width	Count	Description
Ground Floor				
D1	2340	720	1	FLUSH DOOR
D2	2340	820	1	FLUSH DOOR
D2A	2340	720	1	FLUSH DOOR
D3	2340	720	1	FLUSH DOOR
D4	2340	820	1	FLUSH DOOR
D5	2340	720	1	FLUSH DOOR
GD	2400	4800	1	GARAGE DOOR
MD	2340	1200	1	SOLID CORE DOOR
PD1	2340	720	1	POCKET DOOR
SD1	2300	2650	1	SLIDING DOOR

Ground Floor: 10

Level 1

D6	2340	820	1	FLUSH DOOR
D7	2340	820	1	FLUSH DOOR
D8	2340	820	1	FLUSH DOOR
D9	2340	720	1	FLUSH DOOR
D10	2340	820	1	FLUSH DOOR
PD2	2340	720	1	POCKET DOOR
PD3	2340	720	1	POCKET DOOR
PD4	2340	720	1	POCKET DOOR
SD2	2300	2000	1	SLIDING DOOR
SD3	2300	2650	1	SLIDING DOOR

Level 1: 10

CDC ISSUE

REV	DATE	DESCRIPTION	BY
11	Date 11	Glass railing at balcony, LP gas - Ekta/Client	
10	30-07-2026	Metal Railing on Balcony - Developer/Client	
9	28-07-2026	Full Cladding on Front facade on first floor - Bishwas	
8	27-07-2026	Facade Updated with stone and wooden cladding - Bishwas/Sheela	
7	16-07-2026	Metal Railings on balcony - Ekta	

RUBY HOMES



THIS DRAWING IS THE EXCLUSIVE PROPERTY OF THE DEVELOPER & THE REPRODUCTION OF ANY PART WITHOUT THE PRIOR WRITTEN CONSENT OF THE DEVELOPER IS A VIOLATION OF APPLICABLE LAWS. IN NO EVENT SHALL THE DEVELOPER BE HELD LIABLE FOR SPECIAL COLLATERAL, INCIDENTAL OR CONSEQUENTIAL LIABILITY IN CONNECTION WITH THE USE OF THIS DIGITAL DATA ONCE RELEASED FROM THE DEVELOPER'S OFFICE. THIS DRAWING IS TO BE READ & UNDERSTOOD IN CONJUNCTION WITH THE STRUCTURAL, MECHANICAL, ELECTRICAL & / OR ANY OTHER CONSULTANT'S DOCUMENTATION AS MAY BE APPLICABLE TO THE PROJECT PRIOR TO THE START OF ANY WORKS AND FOR ITS DURATION.

PROJECT:
Lot 2088 13 LORIKEET STREET
13 LORIKEET STREET WILTON

DRAWING TITLE:
ELEVATION 01

NORTH:

LOT NO:	DATE:	SCALE:	DRAWING No:	REV:
2088	20-08-2026	1 : 100	CDC.08	11
DRAWN BY:	CHECKED BY:	ISSUED BY:		
AS	RH			
DRAFTED BY:	CLIENT NAME:			
SL	Bhasker Maskey & Sabnam Karki			

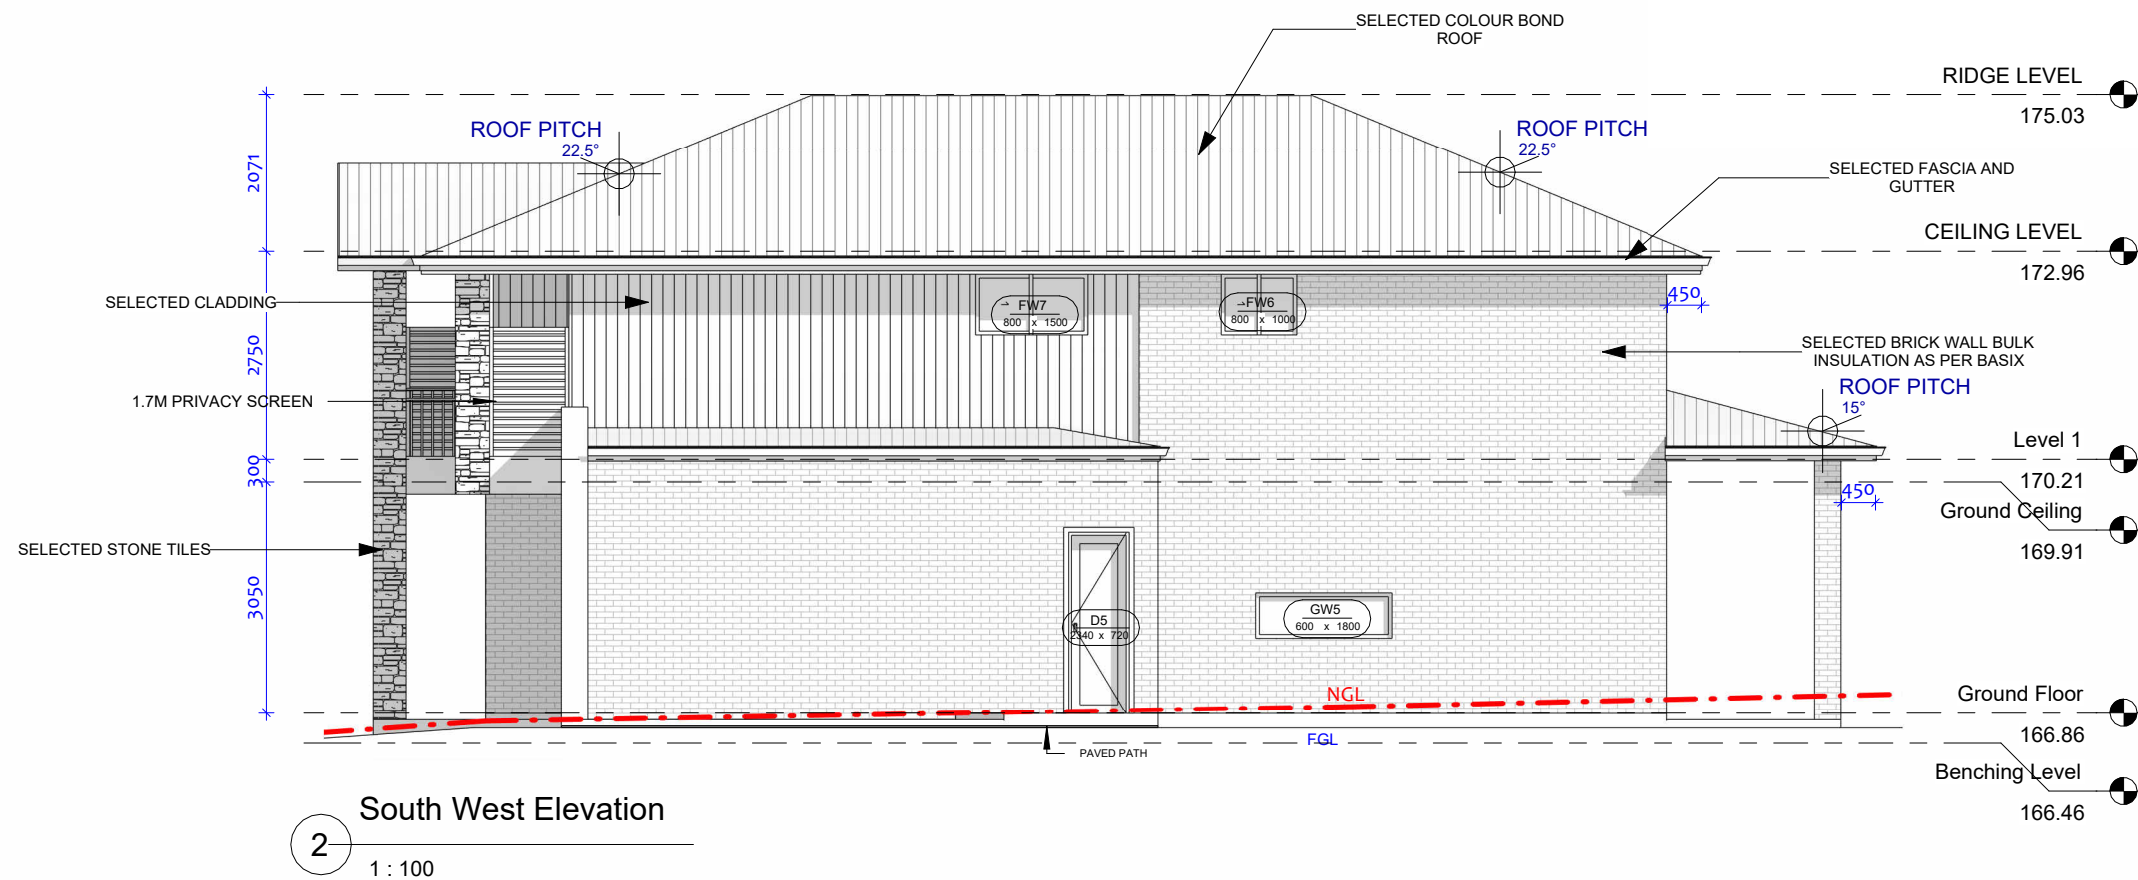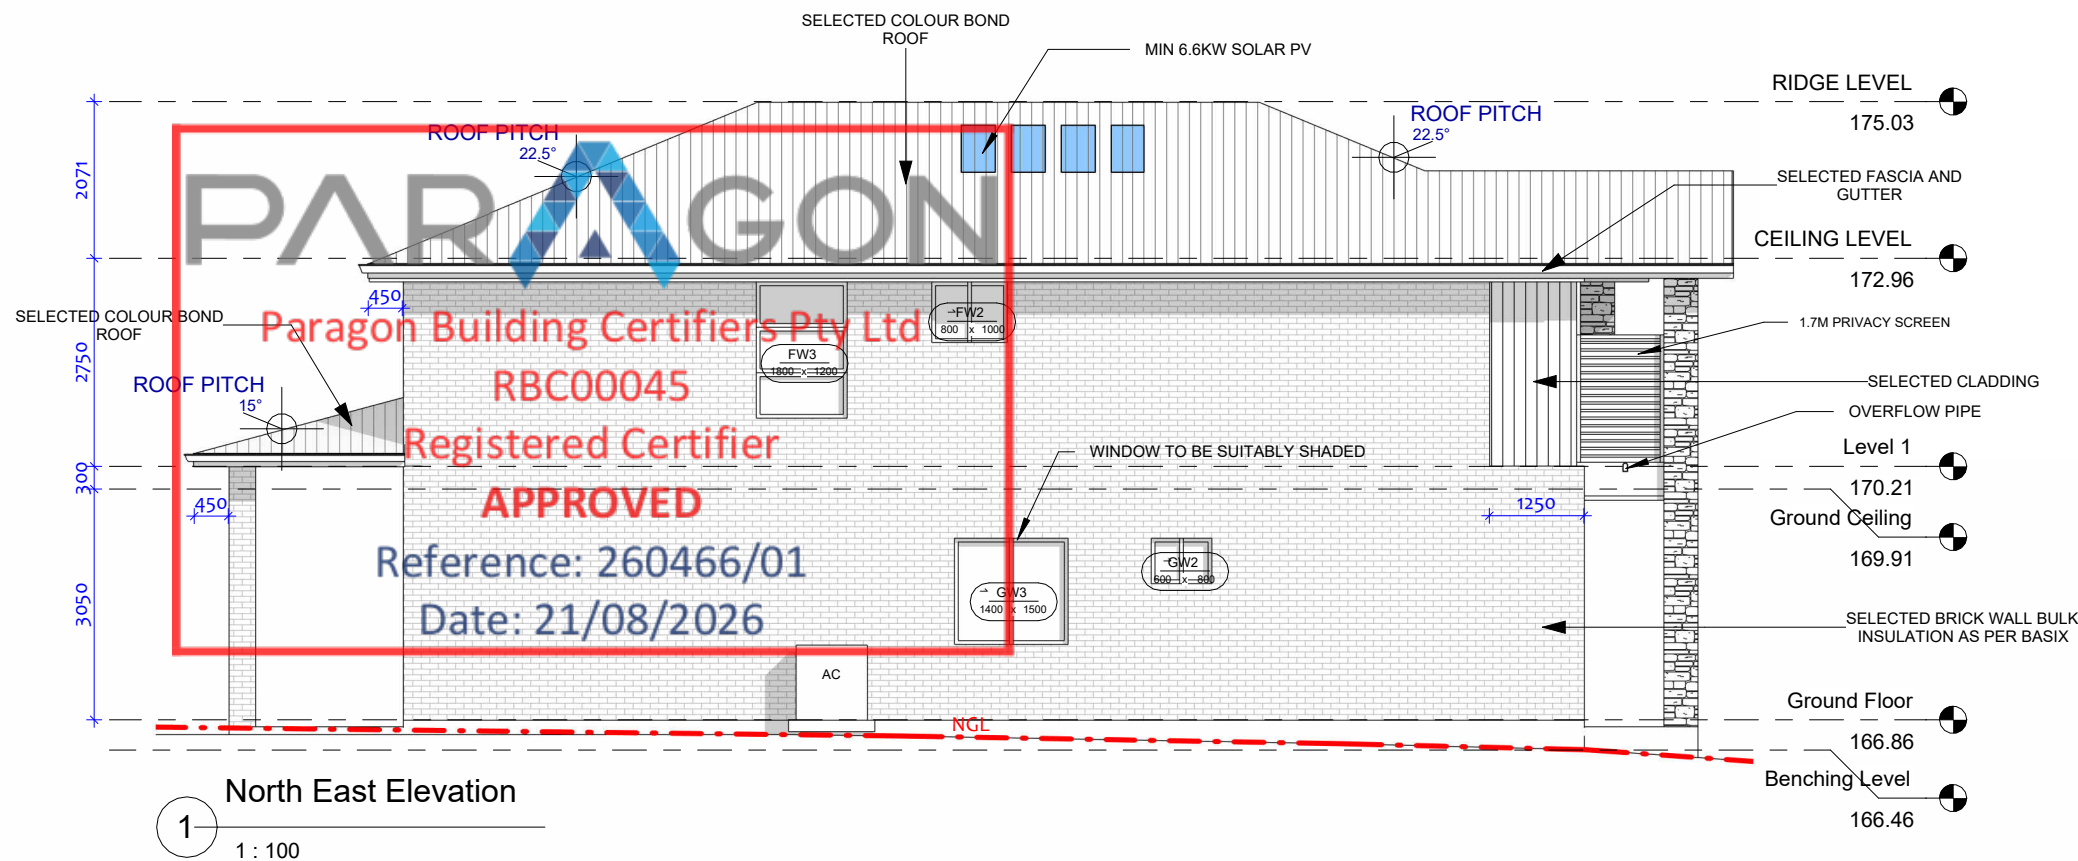

CDC ISSUE			
7	16-07-2026	Metal Railings on balcony - Ekta	
6	15-07-2026	Porch and balcony Extended to 1500mm, balcony above garage reduce to 1500mm, Cladding return on Balcony, Gable Roof on Facade as per developer, All Electric cooktop and Solar added. Area increase to 237 sq.m - Ekta/Developer	
5	25-06-2026	CDC ISSUE	
REV	DATE	DESCRIPTION	BY
 THIS DRAWING IS THE EXCLUSIVE PROPERTY OF THE DEVELOPER & THE REPRODUCTION OF ANY PART WITHOUT THE PRIOR WRITTEN CONSENT OF THE DEVELOPER IS A VIOLATION OF APPLICABLE LAWS. IN NO EVENT SHALL THE DEVELOPER BE HELD LIABLE FOR SPECIAL COLLATERAL, INCIDENTAL OR CONSEQUENTIAL LIABILITY IN CONNECTION WITH THE USE OF THIS DIGITAL DATA ONCE RELEASED FROM THE DEVELOPER'S OFFICE. THIS DRAWING IS TO BE READ & UNDERSTOOD IN CONJUNCTION WITH THE STRUCTURAL, MECHANICAL, ELECTRICAL & / OR ANY OTHER CONSULTANT'S DOCUMENTATION AS MAY BE APPLICABLE TO THE PROJECT PRIOR TO THE START OF ANY WORKS AND FOR ITS DURATION.			
PROJECT:		DRAWING TITLE:	
Lot 2088 13 LORIKEET STREET		ELEVATION 02	
13 LORIKEET STREET WILTON		NORTH:	
LOT NO:	DATE:	SCALE:	DRAWING No:
2088	20-08-2026	1 : 100	CDC.09
DRAWN BY:	CHECKED BY:	ISSUED BY:	
AS	RH	7	
DRAFTED BY:	CLIENT NAME:		
SL	Bhasker Maskey & Sabnam Karki		



Paragon Building Certifiers Pty Ltd


RBC00045

Registered Certifier


APPROVED

Reference: 260466/01

Date: 21/08/2026

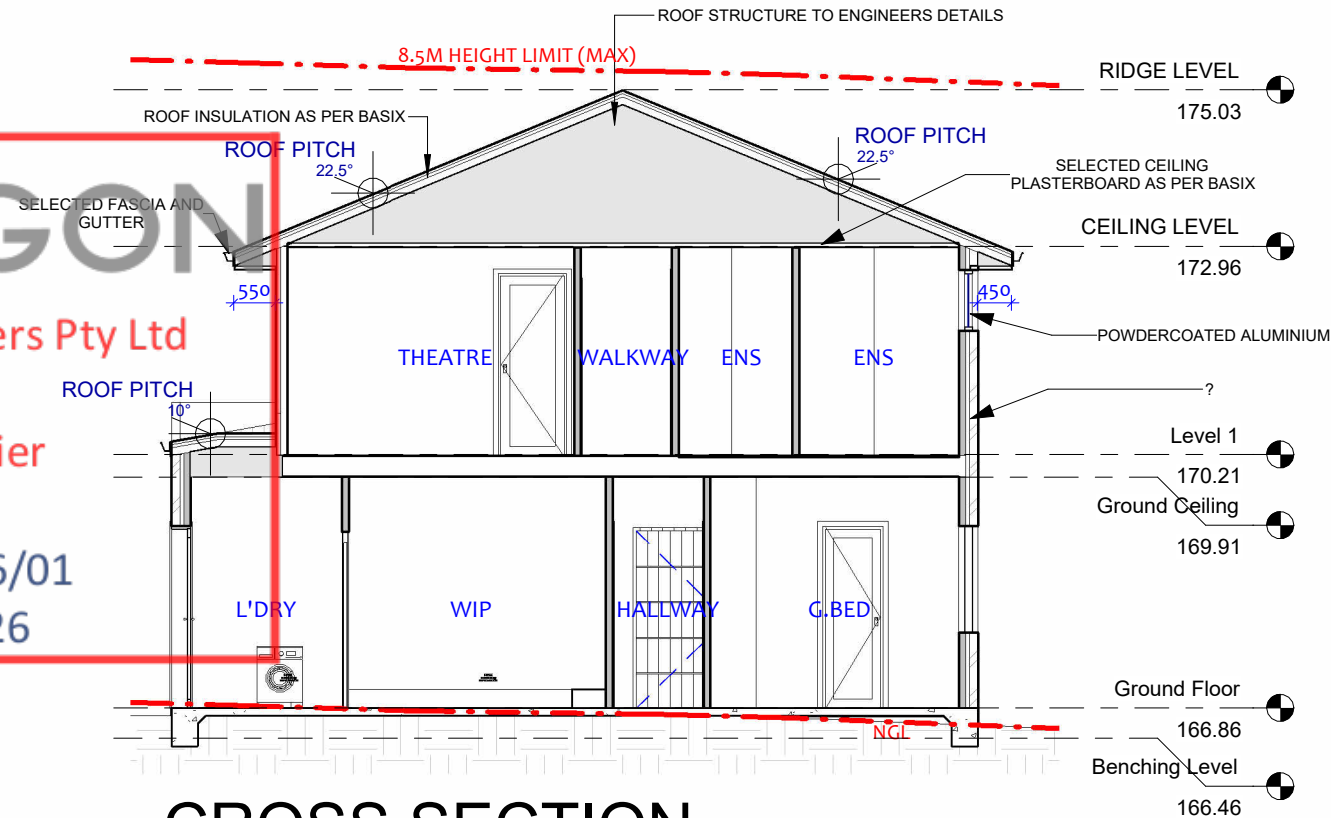

2 CROSS SECTION
1 : 100

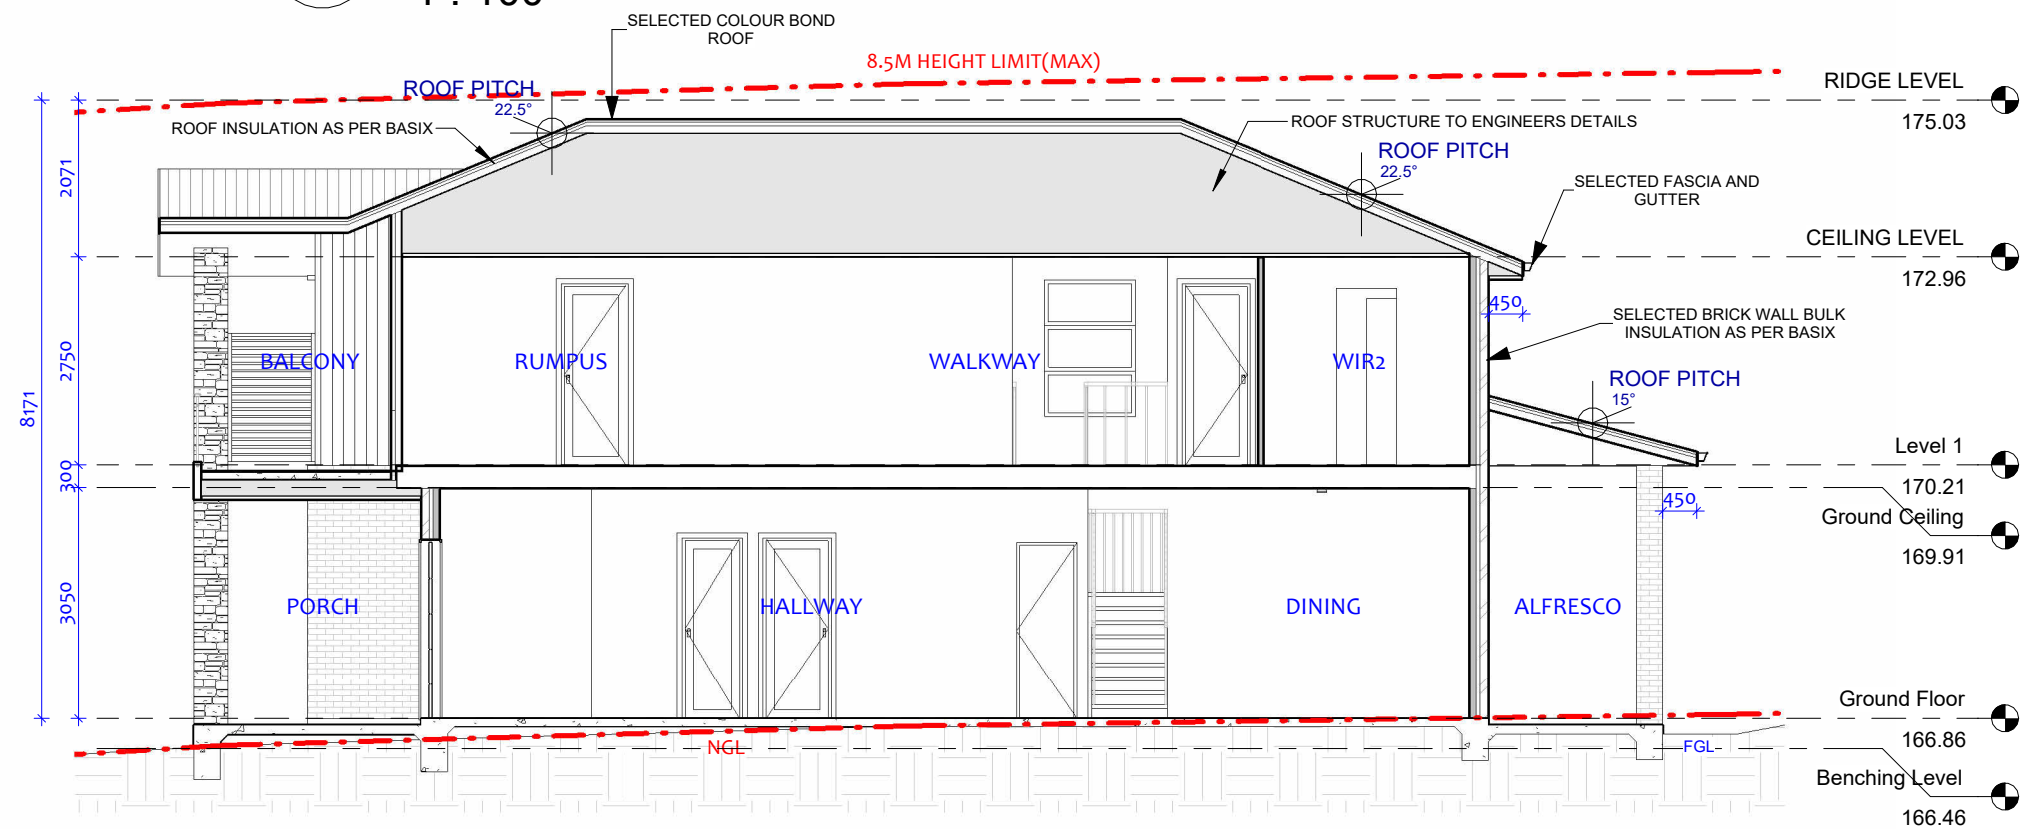

1 LONGITUDINAL SECTION
1 : 100

REV	DATE	DESCRIPTION	BY
6	15-07-2026	Porch and balcony Extended to 1500mm, balcony above garage reduce to 1500mm, Cladding return on Balcony, Gable Roof on Facade as per developer, All Electric cooktop and Solar added. Area increase to 237 sq.m - Ekta/Developer	
5	25-06-2026	CDC ISSUE	


THIS DRAWING IS THE EXCLUSIVE PROPERTY OF THE DEVELOPER & THE REPRODUCTION OF ANY PART WITHOUT THE PRIOR WRITTEN CONSENT OF THE DEVELOPER IS A VIOLATION OF APPLICABLE LAWS. IN NO EVENT SHALL THE DEVELOPER BE HELD LIABLE FOR SPECIAL COLLATERAL, INCIDENTAL OR CONSEQUENTIAL LIABILITY IN CONNECTION WITH THE USE OF THIS DIGITAL DATA ONCE RELEASED FROM THE DEVELOPER'S OFFICE. THIS DRAWING IS TO BE READ & UNDERSTOOD IN CONJUNCTION WITH THE STRUCTURAL, MECHANICAL, ELECTRICAL & / OR ANY OTHER CONSULTANT'S DOCUMENTATION AS MAY BE APPLICABLE TO THE PROJECT PRIOR TO THE START OF ANY WORKS AND FOR ITS DURATION.


PROJECT:
Lot 2088 13 LORIKEET STREET
13 LORIKEET STREET WILTON

DRAWING TITLE:
SECTIONS

NORTH:

LOT NO:	DATE:	SCALE:	DRAWING No:	REV:
2088	20-08-2026	1 : 100	CDC.10	6
DRAWN BY:	CHECKED BY:	ISSUED BY:		
AS	RH			
DRAFTED BY:	CLIENT NAME:			
SL	Bhasker Maskey & Sabnam Karki			

CDC ISSUE

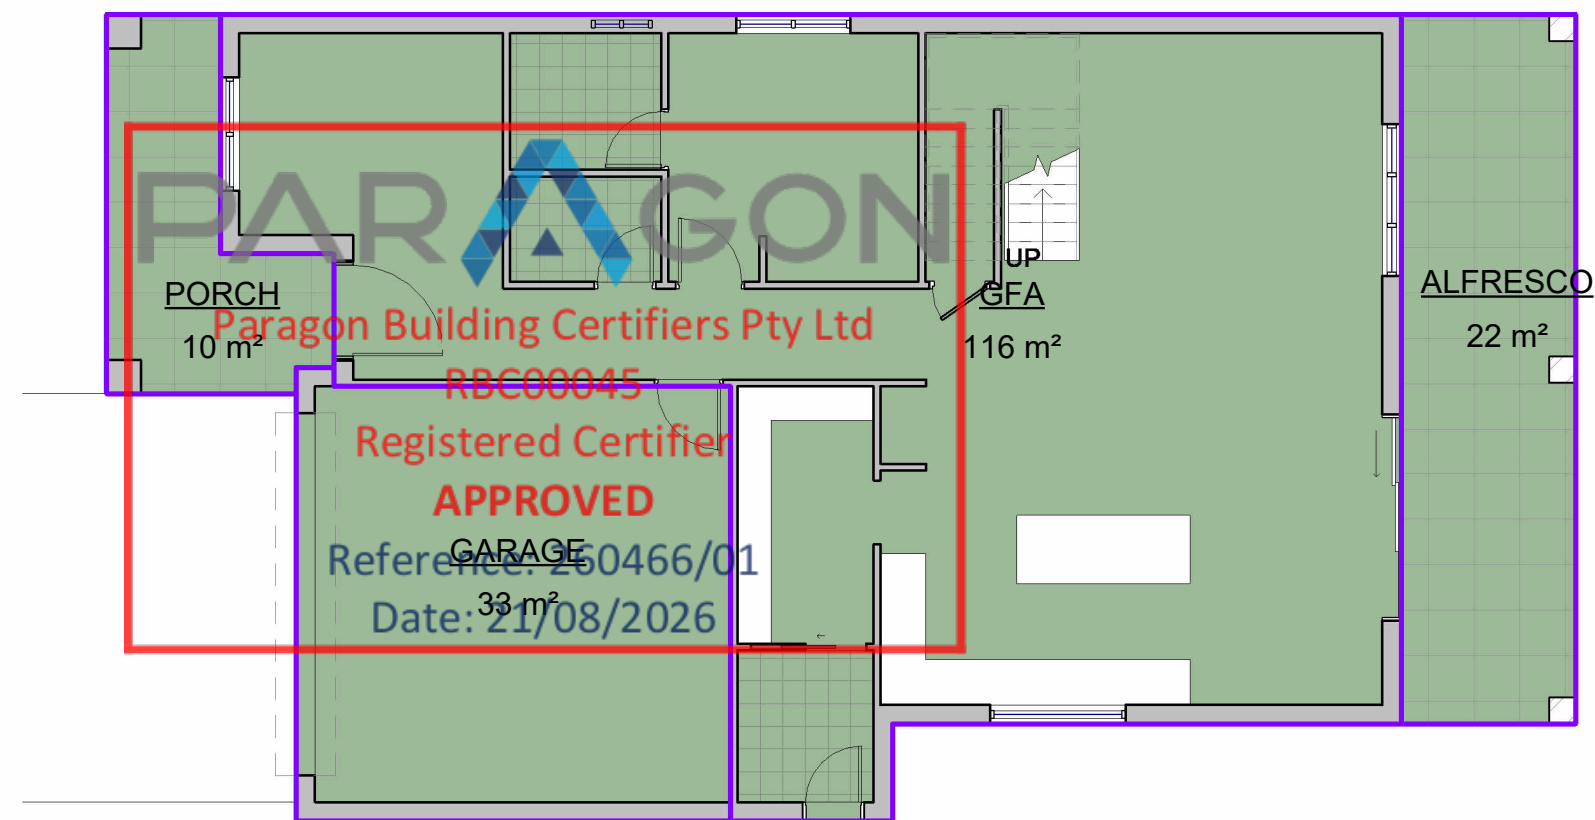

Area Schedule (Gross Building)	
Name	Area

Ground Floor

GFA	116 m ²
PORCH	10 m ²
GARAGE	33 m ²
ALFRESCO	22 m ²

Ground Floor: 4 181 m²


Level 1

FFA	133 m ²
BALCONY	16 m ²
STAIRCASE VOID	6 m ²

Level 1: 3 155 m²

Grand total: 7 336 m²

1 Ground Floor
1 : 100

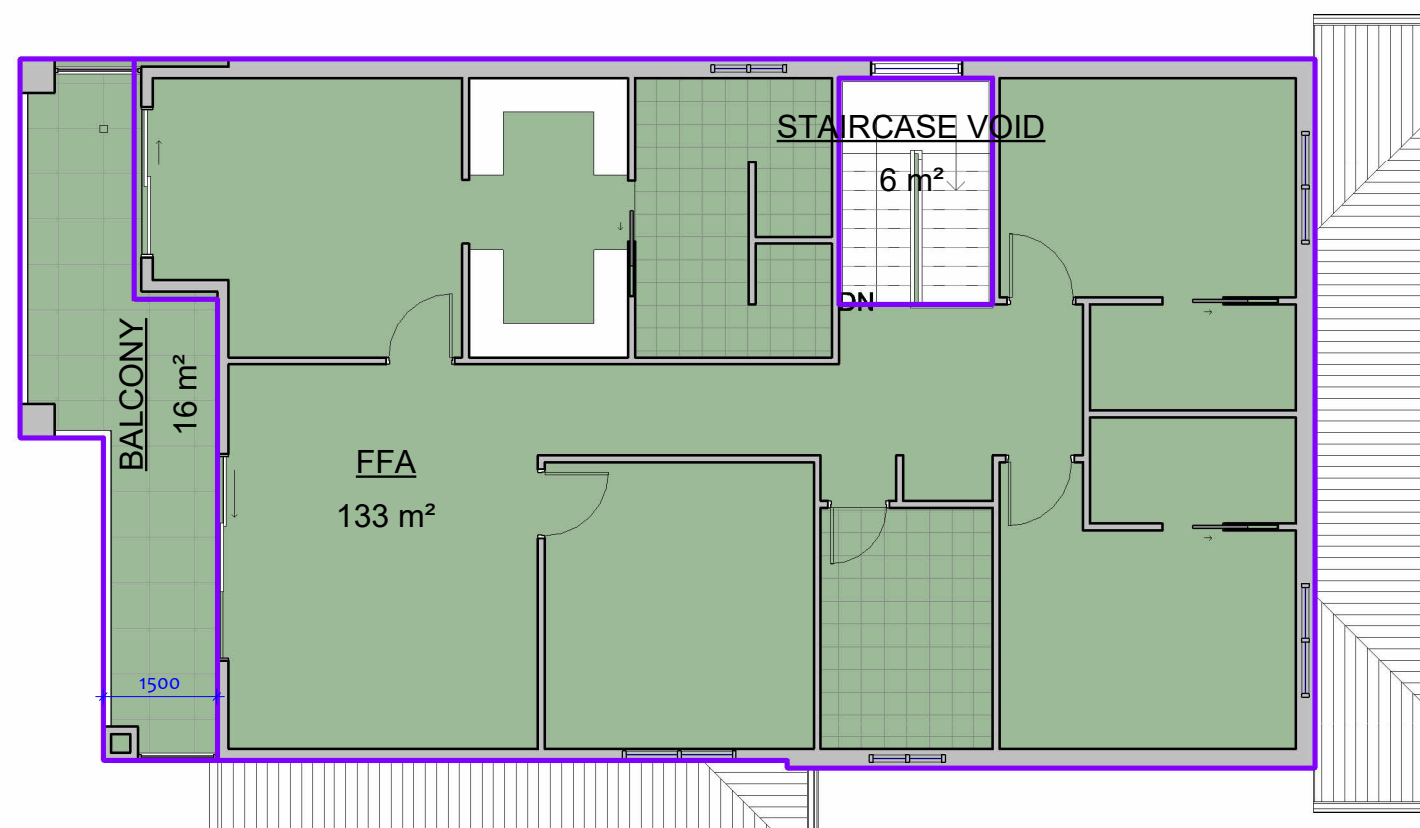


2 Level 1
1 : 100

REV	DATE	DESCRIPTION	BY
6	15-07-2026	Porch and balcony Extended to 1500mm, balcony above garage reduce to 1500mm, Cladding return on Balcony, Gable Roof on Facade as per developer, All Electric cooktop and Solar added. Area increase to 237 sq.m - Ekta/Developer	
5	25-06-2026	CDC ISSUE	


THIS DRAWING IS THE EXCLUSIVE PROPERTY OF THE DEVELOPER & THE REPRODUCTION OF ANY PART WITHOUT THE PRIOR WRITTEN CONSENT OF THE DEVELOPER IS A VIOLATION OF APPLICABLE LAWS. IN NO EVENT SHALL THE DEVELOPER BE HELD LIABLE FOR SPECIAL COLLATERAL, INCIDENTAL OR CONSEQUENTIAL LIABILITY IN CONNECTION WITH THE USE OF THIS DIGITAL DATA ONCE RELEASED FROM THE DEVELOPER'S OFFICE. THIS DRAWING IS TO BE READ & UNDERSTOOD IN CONJUNCTION WITH THE STRUCTURAL, MECHANICAL, ELECTRICAL & / OR ANY OTHER CONSULTANT'S DOCUMENTATION AS MAY BE APPLICABLE TO THE PROJECT PRIOR TO THE START OF ANY WORKS AND FOR ITS DURATION.

PROJECT:
Lot 2088 13 LORIKEET STREET
13 LORIKEET STREET WILTON


DRAWING TITLE:
FLOOR AREA PLAN

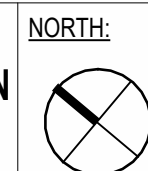

LOT NO: 2088	DATE: 20-08-2026	SCALE: 1 : 100	DRAWING No: CDC.11	REV: 6
DRAWN BY: AS	CHECKED BY: RH		ISSUED BY:	
DRAFTED BY: SL	CLIENT NAME: Bhasker Maskey & Sabnam Karki			

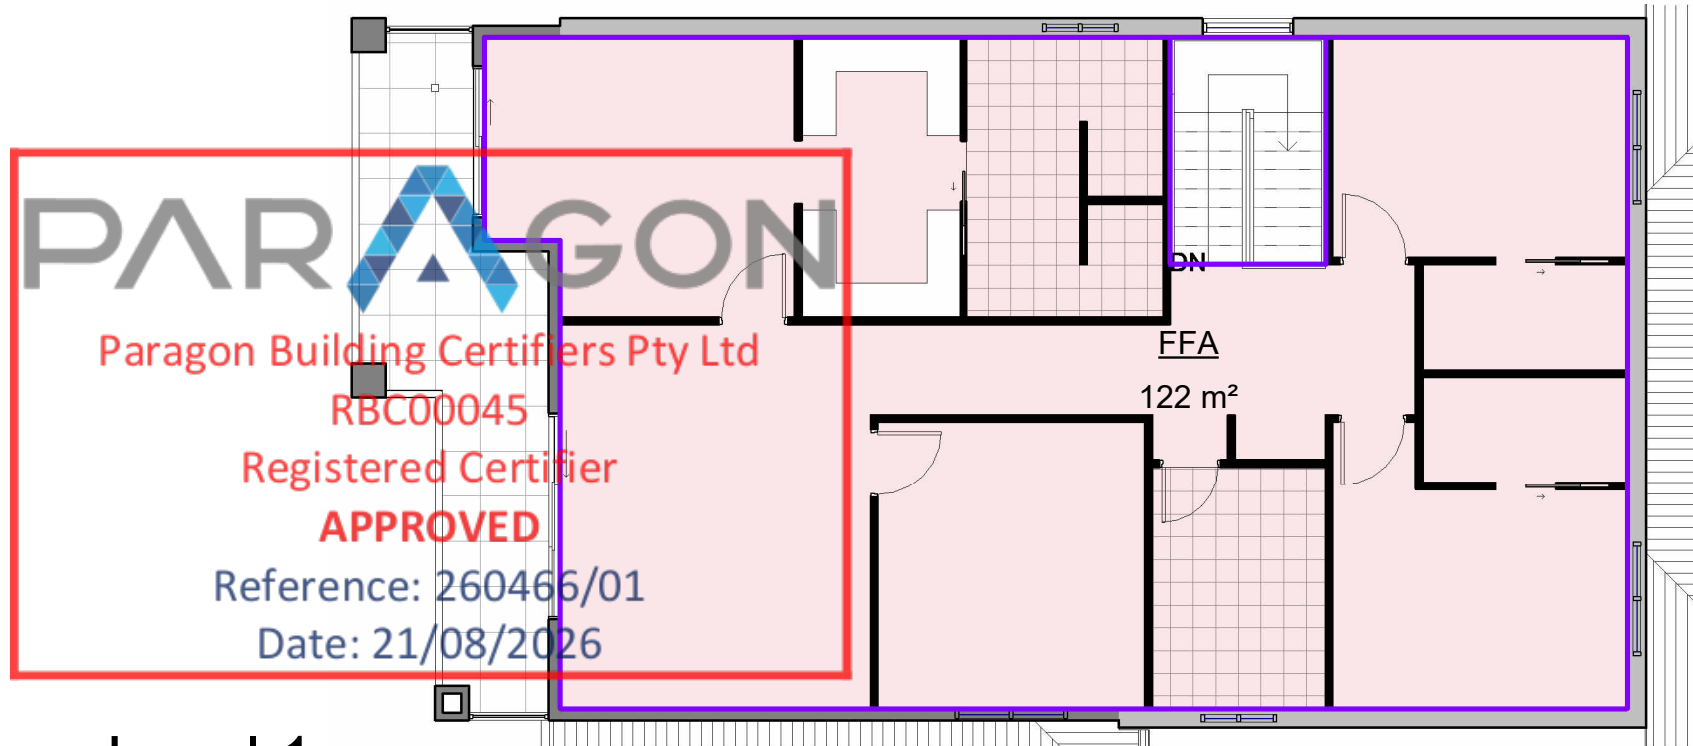

2 Level 1
1 : 100

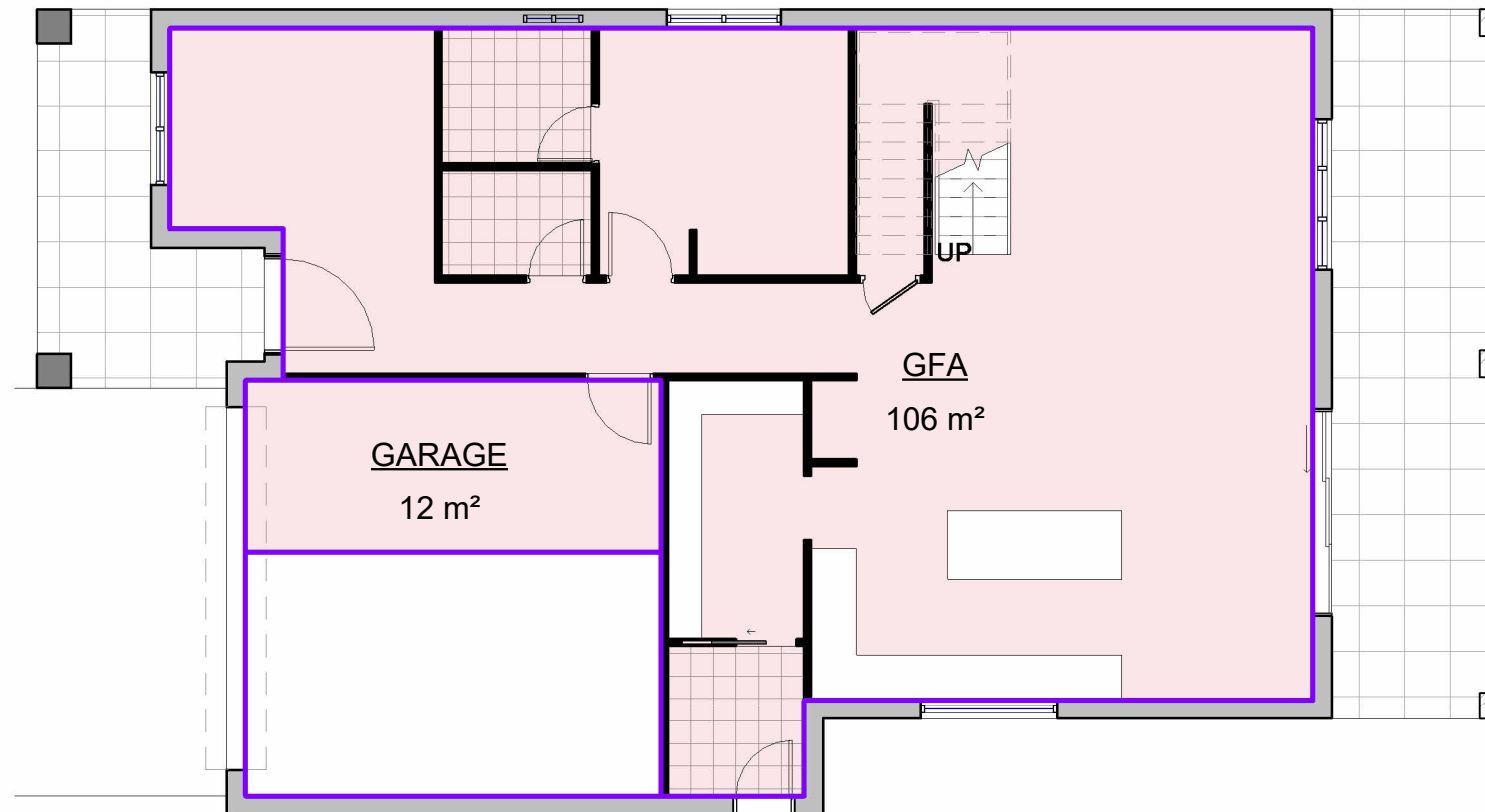

1 Ground Floor
1 : 100

Area Schedule (Rentable)	
Name	Area

Ground Floor	
GFA	106 m ²
GARAGE	12 m ²
Ground Floor: 2	119 m ²
Level 1	
FFA	122 m ²
Level 1: 1	122 m ²
Grand total: 3	241 m ²


				CDC ISSUE								
				 THIS DRAWING IS THE EXCLUSIVE PROPERTY OF THE DEVELOPER & THE REPRODUCTION OF ANY PART WITHOUT THE PRIOR WRITTEN CONSENT OF THE DEVELOPER IS A VIOLATION OF APPLICABLE LAWS. IN NO EVENT SHALL THE DEVELOPER BE HELD LIABLE FOR SPECIAL, COLLATERAL, INCIDENTAL OR CONSEQUENTIAL LIABILITY IN CONNECTION WITH THE USE OF THIS DIGITAL DATA ONCE RELEASED FROM THE DEVELOPER'S OFFICE. THIS DRAWING IS TO BE READ & UNDERSTOOD IN CONJUNCTION WITH THE STRUCTURAL, MECHANICAL, ELECTRICAL & / OR ANY OTHER CONSULTANT'S DOCUMENTATION AS MAY BE APPLICABLE TO THE PROJECT PRIOR TO THE START OF ANY WORKS AND FOR ITS DURATION.	PROJECT: Lot 2088 13 LORIKEET STREET 13 LORIKEET STREET WILTON	DRAWING TITLE: RENTABLE AREA PLAN	NORTH: 	LOT NO: 2088	DATE: 20-08-2026	SCALE: 1 : 100	DRAWING No: CDC.12	REV: 6
DRAWN BY: AS	CHECKED BY: RH	ISSUED BY:										
DRAFTED BY: SL	CLIENT NAME: Bhasker Maskey & Sabnam Karki											
REV	DATE		DESCRIPTION					BY				



THIS DRAWING IS THE EXCLUSIVE PROPERTY OF THE DEVELOPER & THE REPRODUCTION OF ANY PART WITHOUT THE PRIOR WRITTEN CONSENT OF THE DEVELOPER IS A VIOLATION OF APPLICABLE LAWS. IN NO EVENT SHALL THE DEVELOPER BE HELD LIABLE FOR SPECIAL COLLATERAL, INCIDENTAL OR CONSEQUENTIAL LIABILITY IN CONNECTION WITH THE USE OF THIS DIGITAL DATA ONCE RELEASED FROM THE DEVELOPER'S OFFICE. THIS DRAWING IS TO BE READ & UNDERSTOOD IN CONJUNCTION WITH THE STRUCTURAL, MECHANICAL, ELECTRICAL & / OR ANY OTHER CONSULTANT'S DOCUMENTATION AS MAY BE APPLICABLE TO THE PROJECT PRIOR TO THE START OF ANY WORKS AND FOR ITS DURATION.

PARAGON

Paragon Building Certifiers Pty Ltd
RBC00045
Registered Certifier
APPROVED
Reference: 260460/01
Date: 21/08/2026

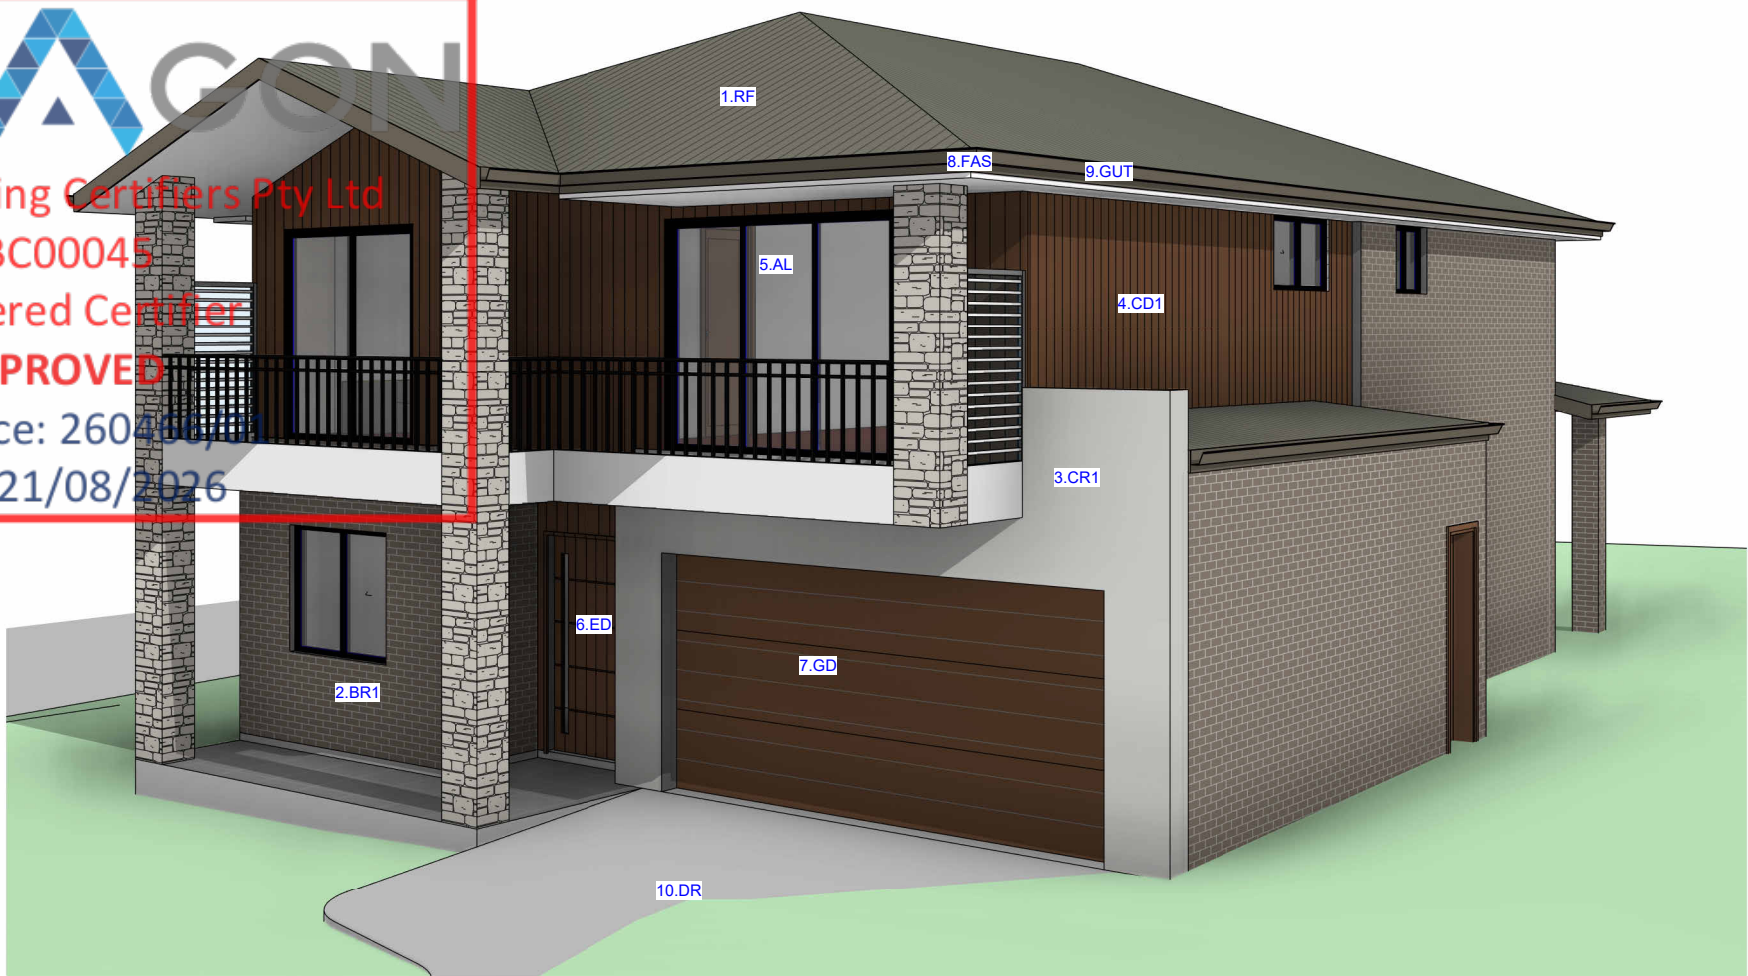

	1. RF	2. BR1	3. CR1	4. CD1	5. AL	6. ED	7. GD	8. FAS	9. GUT	10.DR	10.DR
	ROOF	MAIN WALLS	ACCENT 1/RENDER	CLADDING WALL	WINDOWS/ BALUSTRADE	MAIN DOOR	GARAGE DOOR	FASCIA	GUTTER	DRIVEWAY	STONE
MATERIAL	COLORBOND	BRICK	PAINT ON RENDER	WEATHERBOARD	ALUMINIUM	TIMBER	COLORBOND	COLORBOND	COLORBOND	CONCRETE	TILES
COLOUR											
	DUNE OR SIMILAR (<0.7 SA)	GREY GUM OR SIMILAR	DULUX - WHITE DUNE HALF OR SIMILAR	WEATHERTEX NATURAL CLADDING	MONUMENT OR SIMIAR	WOOD STAIN	JASPER OR SIMILAR	SHALE GREY OR SIMILAR	SHALE GREY OR SIMILAR	SHALE GREY	STONE LOOK TILES

REV	DATE	DESCRIPTION	BY
11	Date 11	Glass railing at balcony, LP gas - Ekta/Client	
10	30-07-2026	Metal Railing on Balcony - Developer/Client	
9	28-07-2026	Full Cladding on Front facade on first floor - Bishwas	
8	27-07-2026	Facade Updated with stone and wooden cladding - Bishwas/Sheela	
7	16-07-2026	Metal Railings on balcony - Ekta	

THIS DRAWING IS THE EXCLUSIVE PROPERTY OF THE DEVELOPER & THE REPRODUCTION OF ANY PART WITHOUT THE PRIOR WRITTEN CONSENT OF THE DEVELOPER IS A VIOLATION OF APPLICABLE LAWS. IN NO EVENT SHALL THE DEVELOPER BE HELD LIABLE FOR SPECIAL COLLATERAL, INCIDENTAL OR CONSEQUENTIAL LIABILITY IN CONNECTION WITH THE USE OF THIS DIGITAL DATA ONCE RELEASED FROM THE DEVELOPER'S OFFICE. THIS DRAWING IS TO BE READ & UNDERSTOOD IN CONJUNCTION WITH THE STRUCTURAL, MECHANICAL, ELECTRICAL & / OR ANY OTHER CONSULTANT'S DOCUMENTATION AS MAY BE APPLICABLE TO THE PROJECT PRIOR TO THE START OF ANY WORKS AND FOR ITS DURATION.

PROJECT:
Lot 2088 13 LORIKEET STREET
13 LORIKEET STREET WILTON

DRAWING TITLE:
COLOR SCHEDULE

NORTH:

LOT NO:
2088

DRAWN BY:
AS

DRAFTED BY:
SL

DATE:
20-08-2026

CHECKED BY:
RH

CLIENT NAME:
Bhasker Maskey & Sabnam Karki



SCALE:
1 : 100

DRAWING No:
CDC.14

REV:
11


ISSUED BY:

CDC ISSUE

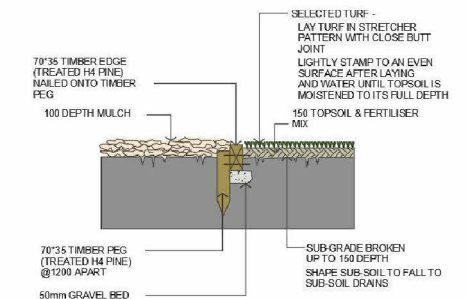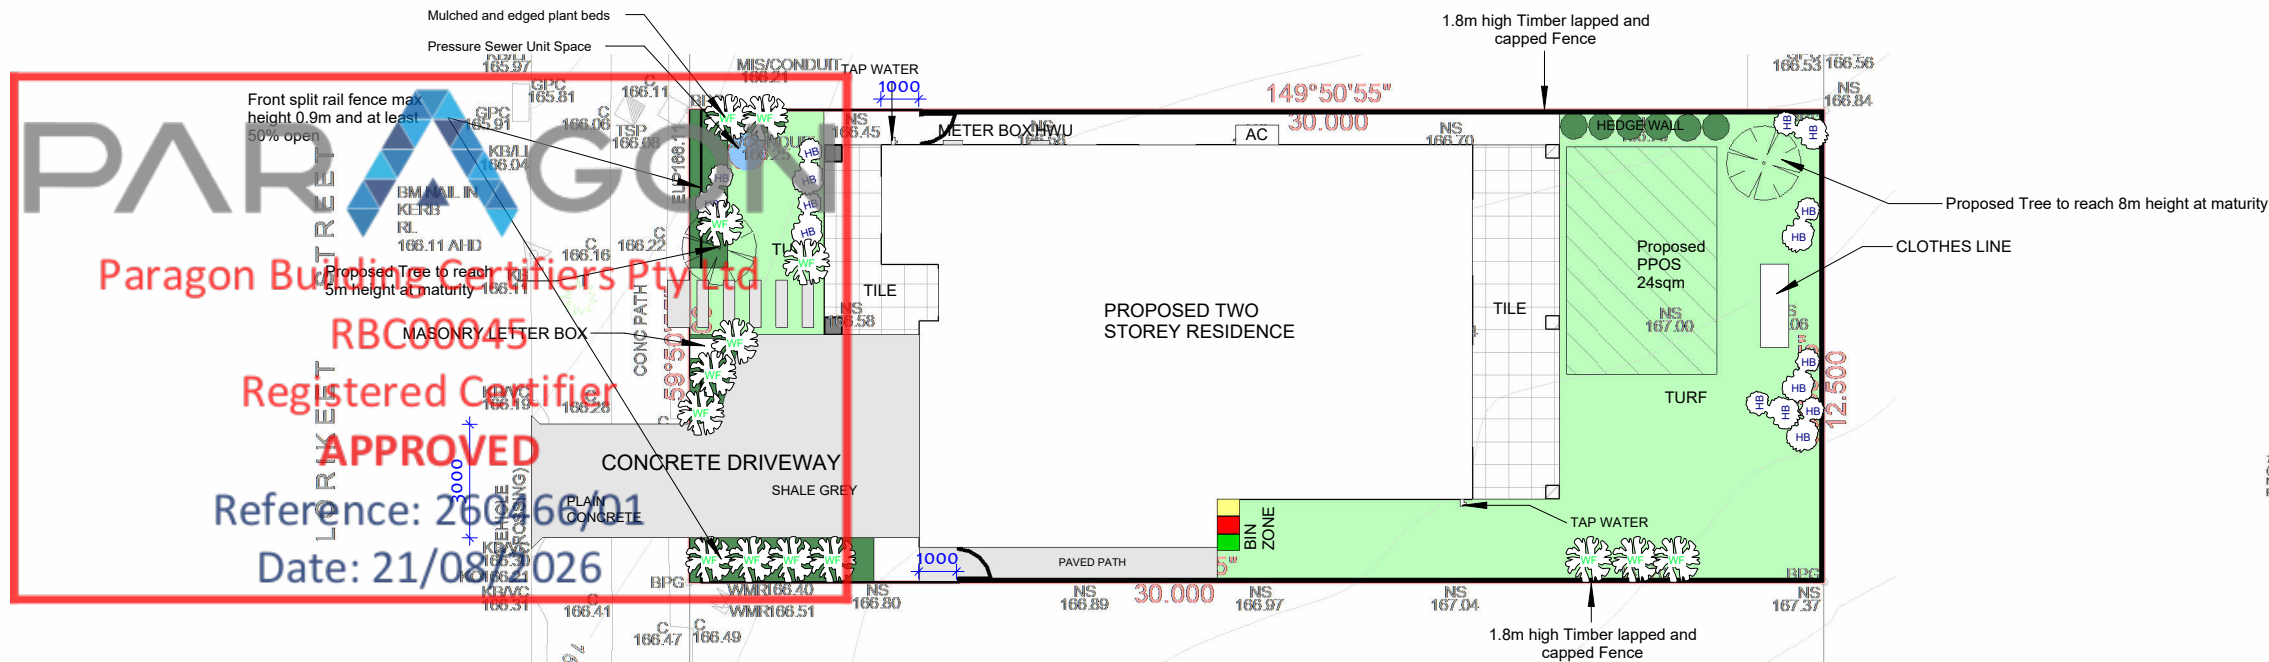

1. TURF & GARDEN EDGE DETAIL

NOTE:
ALIGNMENT OF BRICK EDGE SHALL BE EVEN & FREE FROM
DIPS AND HUMPS

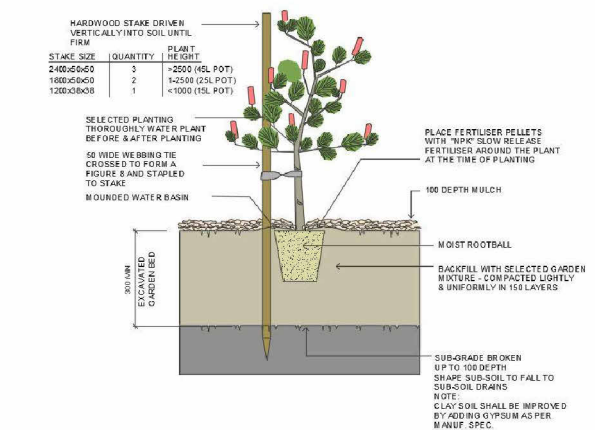

2. TREE & SHRUB PLANTING IN GARDEN BED

NOTE:
DO NOT PLANT IN UNSUITABLE WEATHER CONDITIONS
SUCH AS EXTREME HEAT, COLD, WIND OR RAIN
CLAY SOILS TO BE TREATED WITH CLAY BREAKER
AND ORGANIC COMPOST

CDC - LANDSCAPE PLAN

1
1 : 200

GENERAL NOTES:

- LANDSCAPE CONTRACTOR TO CHECK DA CONDITIONS AND STAMPED LANDSCAPE PLAN
- BEFORE COMMENCING WORKS TO ENSURE NO ADDITIONS/AMENDMENTS TO PLAN
- GARDEN BEDS IN OSD BASIN TO CONSIST OF NON FLOATABLE DECORATIVE GRAVEL.
- REFER TO HYDRAULICS ENGINEERS PLAN FOR OSD DETAILS/FINAL LEVELS.
- MULCHED PLANTING BEDS TO BE A MINIMUM DEPTH OF 75mm AS SELECTED.
- CONTRACTOR'S RESPONSIBILITY TO CHECK AND ADJUST SOIL pH AS REQUIRED.
- PROVIDE TIMBER EDGE AS A MINIMUM BENEATH FENCING/GATES TO DEFINE TURF AND GARDEN BEDS/PATHWAYS, EDGING TO BE PROVIDED TO ALL AREAS WHERE DIFFERING MATERIALS MEET i.e TURF/GARDEN, TURF/GRAVEL PATH ETC.
- WEED MAT BENEATH GRAVEL GRAVEL PATHWAYS REQUIRED TO LIMIT MUD TRACKING.
- PREMIUM ORGANIC GARDEN MIX TO BE USED.
- ALL PLANTS TO BE HEALTHY AND VIGOROUS.
- CONTRACTOR TO MAKE GOOD TURF ON NATURE STRIP POST CONSTRUCTION
- CONTRACTOR TO MAKE GOOD TURF ON NATURE STRIP POST CONSTRUCTION.
- DO NOT SCALE ARCHITECTURAL SETOUT FROM LANDSCAPE DRAWING.
- EXISTING TREE SPREAD APPROXIMATE ONLY. REFER TO TREE REPORT WHEN APPLICABLE.
- SITE SURVEY PROVIDED BY OTHERS.
- BUFFALO TURF PREFERRED OVER KIKUYU.

LANDSCAPE BASIX NOTE:
THE APPLICANT MUST PLANT INDIGENEOUS OR LOW WATER USE SPECIES OF VEGETATION THROUGHOUT 15 SQM OF THE SITE.

NOTE : BUILDER RESERVES THE RIGHT NOT TO UNDERTAKE NOR SUPPLY CERTIFICATE FOR OCCUPATION CERTIFICATE.
NOTE : TO AID COMPLIANCE WITH BASIX LEGISLATION, PLANTS (WHERE APPLICABLE) HAVE BEEN SELECTED FROM THE LOCAL CITY COUNCIL/SHIRE PLANT LISTS.
NOTE: LOCATION OF SEWER MAINS/LINES, WATER PIPES, UNDERGROUND ELECTRICITY AND OTHER SERVICES MUST BE OBTAINED PRIOR TO COMMENCEMENT OF ANY WORK ON SITE.

CONTRACTORS NOTE : CALCULATED AREAS DETERMINED BY CAD AND HAVE BEEN ROUNDED UP FOR USE AS A GUIDE ONLY ALLOW STANDARD PERCENTAGE FOR CUTTING AND WASTAGE .CONFIRM DIMENSIONS AND NUMBERS PRIOR TO QUOTING/ORDERING.

LANDSCAPE AREA	
FRONT AREA	22.7 m ²
BACKYARD AREA	113.35 m ²
TOTAL AREA	136.05 m ²



ZURICH PARCEL MASONRY LETTERBOX
LIGHT GREY COLOUR
CONTEMPORARY STYLE

PLANT SCHEDULE

Genus	Common Name	Qty	Pot size	Height	Planting Height
Trees					
Backhousia myrtifolia	Grey Myrtle	1	75L	6m	1.5m
Betula nigra	Tropical Birch	1	75L	6m	1.5m
Shrubs					
Westringia fruticosa 'Grey Box'	Grey Box Coast Rosemary	13	140mm	1.5m	1m
Banksia spinulosa	Hairpin Banksia	6	140mm	1m	1m
Convolvulus cneorum	Silver Bush	5	140mm	1m	1m
Hedgeing & screening Plants					
Acmena smithii 'Hot Flush'	Hot Flush Lilly Pilly	6	140mm	3m	


REV	DATE	DESCRIPTION	BY
6	15-07-2026	Porch and balcony Extended to 1500mm, balcony above garage reduce to 1500mm, Cladding return on Balcony, Gable Roof on Facade as per developer, All Electric cooktop and Solar added. Area increase to 237 sq.m - Ekta/Developer	
5	25-06-2026	CDC ISSUE	

RUBY HOMES

THIS DRAWING IS THE EXCLUSIVE PROPERTY OF THE DEVELOPER & THE REPRODUCTION OF ANY PART WITHOUT THE PRIOR WRITTEN CONSENT OF THE DEVELOPER IS A VIOLATION OF APPLICABLE LAWS. IN NO EVENT SHALL THE DEVELOPER BE HELD LIABLE FOR SPECIAL COLLATERAL, INCIDENTAL OR CONSEQUENTIAL LIABILITY IN CONNECTION WITH THE USE OF THIS DIGITAL DATA ONCE RELEASED FROM THE DEVELOPER'S OFFICE. THIS DRAWING IS TO BE READ & UNDERSTOOD IN CONJUNCTION WITH THE STRUCTURAL, MECHANICAL, ELECTRICAL & / OR ANY OTHER CONSULTANT'S DOCUMENTATION AS MAY BE APPLICABLE TO THE PROJECT PRIOR TO THE START OF ANY WORKS AND FOR ITS DURATION.

PROJECT:
Lot 2088 13 LORIKEET STREET
13 LORIKEET STREET WILTON

DRAWING TITLE:
LANDSCAPE PLAN

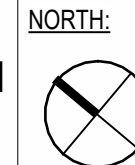

CDC ISSUE					
LOT NO: 2088	DATE: 20-08-2026	SCALE: 1 : 200	DRAWING No: CDC.15	REV: 6	ISSUED BY:
DRAWN BY: AS	CHECKED BY: RH				
DRAFTED BY: SL	CLIENT NAME: Bhasker Maskey & Sabnam Karki				

ABCB HOUSING PROVISIONS : PART 10.2 WET AREA WATERPROOFING

10.2.1 Wet Areas

1.

Building elements in wet areas within a building must be protected with a waterproofing system.
2.

The waterproofing system in (1) must be either waterproof or water resistant in accordance with 10.2.2 to 10.2.6.

10.2.2 Shower Area (enclosed and unenclosed)

1.

For a shower area with a hob, step-down or level threshold, the following applies:

a.

The floor of the shower area must be waterproof, including any hob or step-down (see Figure 10.2.2); and

b.

The walls of the shower area must be waterproof not less than 1800 mm above the floor substrate (see Figure 10.2.2).

c.

Wall junctions and joints within the shower area must be waterproof not less than 40 mm either side of the junction (see Figure 10.2.2).

d.

Wall/floor junctions within the shower area must be waterproof (see Figure 10.2.2).

e.

Penetrations within the shower area must be waterproof.

2.

A shower with a preformed shower base must also comply with the requirements of (1), except for (a) which is not applicable.
- Figure 10.2.2: Extent of treatment for shower areas - concrete compressed fibre-cement and fibre-cement sheet floors.
-
- Figure Notes
Wall/floor junction heights are to be as per 10.2.2 to 10.2.6 (as applicable).
- Notes
Where a shower is above a bath or spa, use requirements for shower.
- 10.2.3 Area outside shower area
1.

For concrete, compressed fibre-cement and fibre-cement sheet flooring, the floor of the room must be water resistant.

2.

For timber floors including particleboard, plywood and other timber based flooring materials, the floor of the room must be waterproof.

3.

Wall/floor junctions must be -

a.

waterproof, and

b.

where a flashing is used, the horizontal leg must be not less than 40 mm.
- 10.2.4 Areas adjacent to baths and spas without showers
1.

For areas adjacent to all baths and spas, the following applies:

a.

For concrete, compressed fibre-cement and fibre-cement sheet flooring, the floor of the room must be water resistant.

b.

For timber floors including particleboard, plywood and other timber based flooring materials, the floor of the room must be waterproof.

c.

Tap and spout penetrations must be waterproof where they occur in horizontal surfaces.

2.

For areas adjacent to non-freestanding baths and spas, the following applies:

a.

Walls must be water resistant (see Figure 10.2.4a and Figure 10.2.4b)-

•

to a height of not less than 150mm above the vessel, for the extent of the vessel, where the vessel is within 75mm of a wall, and

•

for all exposed surfaces below vessel lip.

b.

Wall junctions and joints must be water resistant within 150mm above a vessel for the extent of the vessel.

c.

Wall/floor junctions must be waterproof for the extent of the vessel (see Figure 10.2.4a and Figure 10.2.4b).

3.

For inserted baths and spas, the following applies:

a.

For floors and horizontal surfaces:

•

Any shelf area adjoining the bath or spa must be waterproof and include a waterstop under the vessel lip.

•

There are no requirements for the floor under a bath or spa.

b.

For walls:

•

Waterproof to not less than 150mm above the lip of a bath or spa.

•

There are no requirements for the floor under a bath or spa.

c.

For wall junctions and joints, the following applies:

•

Waterproof junctions within 150mm of a bath or spa.

•

There are no requirements for junctions and joints in walls beneath the lip of a bath or spa.

d.

Tap and spout penetrations must be waterproof where they occur in horizontal surfaces.

Figure 10.2.4a: Areas adjacent to baths and spas without showers for concrete, compressed fibre-cement and fibre-cement sheet flooring

Figure 10.2.4b: Areas adjacent to baths and spas without showers for timber floors including particle-board, plywood and other floor materials

10.2.5 Other areas

1.

For walls adjoining other types of vessels (e.g. sink, basin or laundry tub), the following applies:

a.

Walls must be water resistant to a height of not less than 150mm above the vessel, for the extent of the vessel, where the vessel is within 75 mm of a wall (see Figure 10.2.5.)

b.

Waterproof wall junctions where a vessel is fixed to a wall.

c.

Waterproof tap and spout penetrations where they occur in surfaces required to be waterproof or water resistant.

2.

For laundries and WCs, the following applies:

a.

The floor of the room must be water resistant.

b.

Wall/floor junctions must be water resistant, and where a flashing is used, the horizontal leg must not be less than 40 mm.

3.

For WCs with handheld bidet spray installations, the following applies:

a.

The floor of the room must be waterproof.

b.

Walls must be -

•

waterproof in WC area within a 900 mm radius from the wall connection of the handheld bidet spray device to a height of not less than 150mm above the floor substrate; and

•

water resistant in WC area within a 900 mm radius from the wall connection of the handheld bidet device to not less than 1200 mm above the finished floor level of the WC.

c.

Wall junctions within the WC area within 900 mm radius from the wall connection of the handheld bidet spray device must be waterproof.

d.

Wall/floor junctions within the WC area within 1000 mm radius from the wall connection of the handheld bidet spray device must be waterproof.

e.

Penetrations in the WC area must be waterproof.

Figure 10.2.5: Bath and vessel abutting wall - areas to be protected

10.2.6 Waterproofing systems

1.

For the purposes of this Part, a waterproofing system is deemed -

a.

waterproof, if it complies with (2); or

b.

water resistant, if it complies with (3).

2.

For a waterproofing system required to be waterproof in accordance with 10.2.2 to 10.2.5, the materials nominated in 10.2.8 must be used.

3.

For a waterproofing system required to be water resistant in accordance with 10.2.2 to 10.2.5, the materials nominated in 10.2.9 must be used in conjunction with the materials in 10.2.10.

10.2.12 Construction of wet area floors - falls

Where a floor waste is installed -

a.

the minimum continuous fall of a floor plane to the waste must be 1:80; and

b.

the maximum continuous fall of a floor plane to the waste must be 1:50.

CDC ISSUE																	
5	25-06-2026	CDC ISSUE	BY	PROJECT:	DRAWING TITLE:	NORTH:	LOT NO:	DATE:	SCALE:	DRAWING No:	REV:						
							2088	20-08-2026	1 : 50	CDC.16	5						
							DRAWN BY:	CHECKED BY:			ISSUED BY:						
				Lot 2088 13 LORIKEET STREET 13 LORIKEET STREET WILTON			WATERPROOFING DETAILS		Bhasker Maskey & Sabnam Karki								
							SL										

THIS DRAWING IS THE EXCLUSIVE PROPERTY OF THE DEVELOPER & THE REPRODUCTION OF ANY PART WITHOUT THE PRIOR WRITTEN CONSENT OF THE DEVELOPER IS A VIOLATION OF APPLICABLE LAWS. IN NO EVENT SHALL THE DEVELOPER BE HELD LIABLE FOR SPECIAL COLLATERAL, INCIDENTAL OR CONSEQUENTIAL LIABILITY IN CONNECTION WITH THE USE OF THIS DIGITAL DATA ONCE RELEASED FROM THE DEVELOPER'S OFFICE. THIS DRAWING IS TO BE READ & UNDERSTOOD IN CONJUNCTION WITH THE STRUCTURAL, MECHANICAL, ELECTRICAL & / OR ANY OTHER CONSULTANT'S DOCUMENTATION AS MAY BE APPLICABLE TO THE PROJECT PRIOR TO THE START OF ANY WORKS AND FOR ITS DURATION.

A3