

FOR CONSTRUCTION

LOT 1008 IN DP 1306994

LOCATED AT No.16 Ridgeway Drive Orchard Hills NSW.

Proposed Construction of a New Two-Storey Residential Dwelling with Attached Garage on a Vacant Lot

Paragon Building Certifiers Pty Ltd

RBC00045

Registered Certifier

APPROVED

Reference: 260115/01

Date: 21/08/2026



BASIX™ Certificate

Building Sustainability Index
www.planningportal.nsw.gov.au/development-and-assessment/basix

Single Dwelling

Certificate number: 1835426S_02

This certificate confirms that the proposed development will meet the NSW government's requirements for sustainability, if it is built in accordance with the commitments set out below. Terms used in this certificate, or in the commitments, have the meaning given by the document entitled "BASIX Definitions" dated 10/09/2020 published by the Department. This document is available at www.planningportal.nsw.gov.au/definitions

Secretary
Date of issue: Thursday, 16 April 2026
To be valid, this certificate must be submitted with a development application or lodged with a complying development certificate application within 3 months of the date of issue.



Project summary		
Project name	16 RIDGEWAY DRIVE ORCHARD HILLS, 02	
Street address	16 RIDGEWAY Drive ORCHARD HILLS 2748	
Local Government Area	Penrith City Council	
Plan type and plan number	Deposited Plan DP1306994	
Lot no.	1008	
Section no.	-	
Project type	dwelling house (detached)	
No. of bedrooms	5	
Project score		
Water	✔ 40	Target 40
Thermal Performance	✔ Pass	Target Pass
Energy	✔ 71	Target 70
Materials	✔ -66	Target n/a

Certificate Prepared by	
Name / Company Name: HOMESVALE PTY LTD.	
ABN (if applicable): 76638783150	

BASIX Department of Planning, Housing and Infrastructure www.basix.nsw.gov.au Version: 4.03 / EUCALYPTUS_03_01_0 Certificate No.: 1835426S_02 Thursday, 16 April 2026 page 1/12

GENERAL LEGEND

AC	AIR CONDITIONING UNIT
AL	POWDERCOATED ALUMINIUM DOOR/ WINDOW
BAL	BALUSTRADE TYPE
BG	BOX GUTTER
BR1, BR2, etc.	BRICK FACE TYPE
CAP	METAL CAPPING
CD1, CD2, etc.	WALL CLADDING
CONC.	CONCRETE FLOOR
CPT	CARPET
CRT	CONCRETE ROOF TILES
CR1, CR2, etc.	CEMENT RENDER TYPE/ COLOUR
DP/S	DOWN PIPE
DW	DISH WASHER
ED	ENTRY DOOR
F	FRIDGE
FAS	FASCIA
FET	FEATURE TILE
FT, FT1, FT2, etc.	FLOOR TILES
FW	FLOOR WASTE
GD	GARAGE DOOR
GUT	GUTTER
HWU	HOT WATER UNIT
HYB	HYBRID FLOOR
L	LINEN
MR	METAL ROOF
MW	MICROWAVE OVEN
NGL	NATURAL GROUND LEVEL
OBS	OBSCURED GLASS
P	PANTRY
R	ROBE
RL	REDUCED LEVEL
RWH	RAIN WATER HEAD
RWT	RAIN WATER TANK
S	STORAGE
TOW	TOP OF WALL
TL	TIMBER LAMINATE
WC	WATER CLOSET
WM	WASHING MACHINE
SD	SMOKE DETECTOR

Sheet List

Sheet No.	Sheet Name	Drawn By	Current Revision Date	Revision
CC.01	COVER SHEET	AS	31-07-2026	CC ISSUE
CC.02A	GENERAL NOTES	AS	31-07-2026	CC ISSUE
CC.02B	GENERAL NOTES	AS	31-07-2026	CC ISSUE
CC.03A	LOCATION PLAN AND SITE PLAN	AS	31-07-2026	CC ISSUE
CC.03B	SITE CUT/FILL	AS	31-07-2026	CC ISSUE
CC.04	SITE ANALYSIS AND SEDIMENT CONTROL	AS	31-07-2026	CC ISSUE
CC.05	GROUND FLOOR PLAN	AS	31-07-2026	CC ISSUE
CC.06	FIRST FLOOR LEVEL	AS	31-07-2026	CC ISSUE
CC.07	ROOF PLAN	AS	31-07-2026	CC ISSUE
CC.08	ELEVATION 01	AS	31-07-2026	CC ISSUE

Sheet List

Sheet No.	Sheet Name	Drawn By	Current Revision Date	Revision
CC.09	ELEVATION 02	AS	31-07-2026	CC ISSUE
CC.10	SECTIONS	AS	31-07-2026	CC ISSUE
CC.11	FLOOR AREA PLAN	AS	31-07-2026	CC ISSUE
CC.12	RENTABLE AREA PLAN	AS	31-07-2026	CC ISSUE
CC.13	ROOM AREA PLAN	AS	31-07-2026	CC ISSUE
CC.14	COLOR SCHEDULE	AS	31-07-2026	CC ISSUE
CC.15	LANDSCAPE PLAN	AS	31-07-2026	CC ISSUE
CC.16	WATERPROOFING DETAILS	AS	31-07-2026	CC ISSUE
CC.18	BASIX	AS	31-07-2026	CC ISSUE

NOTE.: ALL IMAGES ARE FOR ILLUSTRATION ONLY AND ARE SUBJECT TO VARIATION AND TO AVAILABILITY OF MATERIALS.

REV	DATE	DESCRIPTION	BY
5	31-07-2026	CC ISSUE	
4	29-06-2026	RFI 3 ISSUE	
3	16-06-2026	RFI 2 ISSUE	
2	26-05-2026	RFI ISSUE	
1	22-04-2026	DA ISSUE	

THIS DRAWING IS THE EXCLUSIVE PROPERTY OF THE DEVELOPER & THE REPRODUCTION OF ANY PART WITHOUT THE PRIOR WRITTEN CONSENT OF THE DEVELOPER IS A VIOLATION OF APPLICABLE LAWS. IN NO EVENT SHALL THE DEVELOPER BE HELD LIABLE FOR SPECIAL COLLATERAL, INCIDENTAL OR CONSEQUENTIAL LIABILITY IN CONNECTION WITH THE USE OF THIS DIGITAL DATA ONCE RELEASED FROM THE DEVELOPER'S OFFICE. THIS DRAWING IS TO BE READ & UNDERSTOOD IN CONJUNCTION WITH THE STRUCTURAL, MECHANICAL, ELECTRICAL & / OR ANY OTHER CONSULTANT'S DOCUMENTATION AS MAY BE APPLICABLE TO THE PROJECT PRIOR TO THE START OF ANY WORKS AND FOR ITS DURATION.

PROJECT:
Residential Dwelling

LOT 1008 IN DP 1306994
LOCATED AT No.16 Ridgeway
Drive Orchard Hills NSW.

DRAWING TITLE:
COVER SHEET

NORTH:

LOT NO:	DATE:	SCALE:	DRAWING No:	REV:
1008	11-08-2026	1 : 100	CC.01	5
DRAWN BY:	CHECKED BY:			ISSUED BY:
AS	RH			
DRAFTED BY:	CLIENT NAME:			
SL	Saggita Reddy			

CC ISSUE

BUILDING SPECIFICATIONS

**National Construction Code – Volume 2,
Amendment 1 – Building Code of Australia 2022
& Housing Provisions Standard 2022**

SITE PREPARATION

- PART 3.1 OF THE NCC VOLUME 2, AMENDMENT 1 - BUILDING CODE OF AUSTRALIA 2022 & HOUSING PROVISIONS STANDARD 2022.

EARTHWORKS

- TO BE CARRIED OUT IN ACCORDANCE WITH THE REQUIREMENTS OF THE ENVIRONMENTAL PLANNING & ASSESSMENT ACT 1979 AND DEVELOPMENT CONSENT CONDITIONS
- PART 3.2 OF THE NCC VOLUME 2, AMENDMENT 1 - BUILDING CODE OF AUSTRALIA 2022 & HOUSING PROVISIONS STANDARD 2022.
- AS 4678:2002 - EARTH-RETAINING STRUCTURES

DRAINAGE

- PART 3.3 OF THE NCC VOLUME 2, AMENDMENT 1 - BUILDING CODE OF AUSTRALIA 2022 & HOUSING PROVISIONS STANDARD 2022.
- AS/NZS 3500.1:2021 - PLUMBING & DRAINAGE - WATER SERVICES
- AS/NZS 3500.2:2021 - PLUMBING & DRAINAGE - SANITARY PLUMBING & DRAINAGE
- AS/NZS 3500.3:2021 - PLUMBING & DRAINAGE STORMWATER DRAINAGE
- AS/NZS 3500.4:2021 - PLUMBING & DRAINAGE - HEATED WATER SERVICES

STRUCTURAL WORK

- Part 2.2 OF THE NCC VOLUME 2, AMENDMENT 1 - BUILDING CODE OF AUSTRALIA 2022 & HOUSING PROVISIONS STANDARD 2022.
- AS 4100-2020– STEEL STRUCTURES CODES
- AS/NZS 1170.0-2002 – GENERAL PRINCIPLES
- ASNZS 1170.1-2002 – PARTS 1 PERMANENT, IMPOSED AND OTHER ACTIONS
- AS/NZS 1170.2-2021 – PART 2 WIND ACTIONS
- AS 3700-2018– SAA MASONRY CODE
- AS 1684.3-2021- RESIDENTIAL TIMBER FRAMED CONSTRUCTION

FOOTINGS & SLABS

- PART 4 OF THE NCC VOLUME 2, AMENDMENT 1 - BUILDING CODE OF AUSTRALIA 2022 & HOUSING PROVISIONS STANDARD 2022.
- AS 2159:2009 - PILING - DESIGN & INSTALLATION
- AS 2870:2011 - RESIDENTIAL SLABS & FOOTINGS
- AS 3600:2018 - CONCRETE STRUCTURES

MASONRY

- PART 5 OF THE NCC VOLUME 2, AMENDMENT 1 - BUILDING CODE OF AUSTRALIA 2022 & HOUSING PROVISIONS STANDARD 2022.
- AS 3700:2018 - MASONRY STRUCTURES

FRAMING

- PART 6 OF THE NCC VOLUME 2, AMENDMENT 1 - BUILDING CODE OF AUSTRALIA 2022 & HOUSING PROVISIONS STANDARD 2022.
- AS 1684.2:2021 - RESIDENTIAL TIMBER-FRAMED CONSTRUCTION - NON- CYCLONIC AREAS
- AS 1720.1:2010 - TIMBER STRUCTURES - DESIGN METHODS
- AS 4100:2020 - STEEL STRUCTURES
- AS 3660.1-2014 – TERMITE MANAGEMENT SYSTEM

ROOF & WALL CLADDING

- PART 7 OF THE NCC VOLUME 2, AMENDMENT 1 - BUILDING CODE OF AUSTRALIA 2022 & HOUSING PROVISIONS STANDARD 2022.
- AS 1273:1991 - UNPLASTICIZED PVC (UPVC) DOWNPIPES & FITTINGS FOR RAINWATER
- AS 1562.1:2018 - DESIGN & INSTALLATION OF SHEET ROOF & WALL CLADDING - METAL
- AS/NZS 1562.3:2006 - DESIGN & INSTALLATION OF SHEET ROOF & WALL CLADDING - PLASTIC
- AS 2049:2002 - ROOF TILES
- AS 2050:2018 - INSTALLATION OF ROOF TILES
- AS 4285:2019 – ROOFLIGHTS

GLAZING

- PART 8 OF THE NCC VOLUME 2, AMENDMENT 1 - BUILDING CODE OF AUSTRALIA 2022 & HOUSING PROVISIONS STANDARD 2022.
- AS 1288:2021 - GLASS IN BUILDINGS - SELECTION & INSTALLATION
- AS 2047:2014 - WINDOWS & EXTERNAL GLAZED DOORS IN BUILDINGS
- AS/NZS 2208:1996 - SAFETY GLAZING MATERIALS IN BUILDINGS

FIRE SAFETY

- PART 9 OF THE NCC VOLUME 2, AMENDMENT 1 - BUILDING CODE OF AUSTRALIA 2022 & HOUSING PROVISIONS STANDARD 2022.
- AS 3786:2014 - SMOKE ALARMS USING SCATTERED LIGHT, TRANSMITTED LIGHT OR IONIZATION

HEALTH & AMENITY

- PART 10 OF THE NCC VOLUME 2, AMENDMENT 1 - BUILDING CODE OF AUSTRALIA 2022 & HOUSING PROVISIONS STANDARD 2022.
- AS/NZS ISO 717.1:2004 - ACOUSTICS - RATING OF SOUND INSULATION IN BUILDINGS & OF BUILDING ELEMENTS - AIRBORNE SOUND INSULATION
- AS ISO 717.2:2004 - ACOUSTICS - RATING OF SOUND INSULATION IN BUILDINGS & OF BUILDING ELEMENTS - IMPACT SOUND INSULATION
- AS 1668.2:2012 - THE USE OF VENTILATION & AIR CONDITIONING IN BUILDINGS - MECHANICAL VENTILATION IN BUILDINGS
- AS 1668.4:2012 - THE USE OF VENTILATION & AIR CONDITIONING IN BUILDINGS - NATURAL VENTILATION OF BUILDINGS
- AS/NZS 1680.0:2009 - INTERIOR LIGHTING - SAFE MOVEMENT
- AS 3740:2021 - WATERPROOFING OF DOMESTIC WET AREAS
- AS 3000-2018 – ELECTRICAL INSTALLATION
- BCA Part 10.8.1, AS4200.1 & AS4200.2 – PLIABLE BUILDING MEMBRANE INSTALLED.

WATERPROOFING

- PART 10.2 OF THE NCC VOLUME 2, AMENDMENT 1 - BUILDING CODE OF AUSTRALIA 2022 & HOUSING PROVISIONS STANDARD 2022
- AS 3740-2021– WATERPROOFING TO WET AREA
- AS 4654-2012 – EXTERNAL WET AREAS

SAFE MOVEMENT & ACCESS

- PART 11 OF THE NCC VOLUME 2, AMENDMENT 1 - BUILDING CODE OF AUSTRALIA 2022 & HOUSING PROVISIONS STANDARD 2022.
- AS 1428.1:2009 - DESIGN FOR ACCESS & MOBILITY – GENERAL REQUIREMENTS FOR ACCESS - NEW BUILDING WORK
- AS 1657:2018 - FIXED PLATFORMS, WALKWAYS, STAIRWAYS & LADDERS - DESIGN, CONSTRUCTION & INSTALLATION

HANDRAILS & BALUSTRADE

- PART 11.3.3 OF THE NCC VOLUME 2, AMENDMENT 1 - BUILDING CODE OF AUSTRALIA 2022 & HOUSING PROVISIONS STANDARD 2022.
- PART 11.3.4 OF THE NCC VOLUME 2, AMENDMENT 1 - BUILDING CODE OF AUSTRALIA 2022 & HOUSING PROVISIONS STANDARD 2022.
- PART 11.3.5 OF THE NCC VOLUME 2, AMENDMENT 1 - BUILDING CODE OF AUSTRALIA 2022 & HOUSING PROVISIONS STANDARD 2022.
- AS 1170.1-2002 – BALUSTRADE INSTALLATION

PROTECTION OF OPENABLE WINDOW

PART 11.3.7 AND 11.3.8 OF THE NCC VOLUME 2, AMENDMENT 1 - BUILDING CODE OF AUSTRALIA 2022 & HOUSING PROVISIONS STANDARD 2022.

ENERGY EFFICIENCY

- PART 13 OF THE NCC VOLUME 2, AMENDMENT 1 - BUILDING CODE OF AUSTRALIA 2022 & HOUSING PROVISIONS STANDARD 2022 & BASIX CERTIFICATE.

HEATING APPLIANCES, FIREPLACES, CHIMNEYS AND FLUES

- PART 12.4 OF THE NCC VOLUME 2, AMENDMENT 1 - BUILDING CODE OF AUSTRALIA 2022 & HOUSING PROVISIONS STANDARD 2022.

MECHANICAL VENTILATION

- EXHAUST FROM A BATHROOM, SANITARY COMPARTMENT TO DISCHARGE DIRECTLY TO OUTDOOR AIR WITH MINIMUM FLOW RATE OF 25L/S & MAKE-UP AIR VIA OPENINGS TO AN ADJACENT ROOM WITH A FREE AREA OF 14,000 MM². THIS EXHAUST SYSTEM MUST BE INTERLOCKED WITH LIGHT SWITCH AND INCLUDE RUN-ON TIMER SO THAT THE EXHAUST SYSTEM CONTINUES TO OPERATE FOR 10 MINUTES AFTER THE LIGHT SWITCH IS OFF.
- ANY INSTALLED - KITCHEN RANGEHOOD EXHAUST TO DISCHARGE DIRECTLY OR VIA DUCT TO OUTDOOR AIR WITH MINIMUM FLOW RATE OF 40L/S & MAKE-UP AIR VIA OPENINGS TO AN ADJACENT ROOM WITH A FREE AREA OF 14,000 MM².
- LAUNDRY EXHAUST TO DISCHARGE DIRECTLY OR VIA DUCT TO OUTDOOR AIR WITH MINIMUM FLOW RATE OF 40L/S & MAKE-UP AIR VIA OPENINGS TO AN ADJACENT ROOM WITH A FREE AREA OF 14,000 MM².



CC ISSUE

REV	DATE	DESCRIPTION	BY
5	31-07-2026	CC ISSUE	
4	29-06-2026	RFI 3 ISSUE	
3	16-06-2026	RFI 2 ISSUE	
2	20-06-2026	RFI 1 ISSUE	
1	22-04-2026	DA ISSUE	



THIS DRAWING IS THE EXCLUSIVE PROPERTY OF THE DEVELOPER & THE REPRODUCTION OF ANY PART WITHOUT THE PRIOR WRITTEN CONSENT OF THE DEVELOPER IS A VIOLATION OF APPLICABLE LAWS. IN NO EVENT SHALL THE DEVELOPER BE HELD LIABLE FOR SPECIAL COLLATERAL, INCIDENTAL OR CONSEQUENTIAL LIABILITY IN CONNECTION WITH THE USE OF THIS DIGITAL DATA ONCE RELEASED FROM THE DEVELOPER'S OFFICE. THIS DRAWING IS TO BE READ & UNDERSTOOD IN CONJUNCTION WITH THE STRUCTURAL, MECHANICAL, ELECTRICAL & / OR ANY OTHER CONSULTANT'S DOCUMENTATION AS MAY BE APPLICABLE TO THE PROJECT PRIOR TO THE START OF ANY WORKS AND FOR ITS DURATION.

PROJECT:
Residential Dwelling

**LOT 1008 IN DP 1306994
LOCATED AT No.16 Ridgeway
Drive Orchard Hills NSW.**


DRAWING TITLE:
GENERAL NOTES

NORTH:

LOT NO:	DATE:	SCALE:	DRAWING No:	REV:
1008	11-08-2026	1 : 2	CC.02A	5
DRAWN BY:	CHECKED BY:			ISSUED BY:
AS	RH			
DRAFTED BY:	CLIENT NAME:			
SL	Saggita Reddy			


TERMITE SHEET

- TERMITE SHEET EXTENDS THROUGH THE ENTIRE MASONRY LEAF AND IS VISIBLE AT THE FINISHED FACE OF THE WALL.

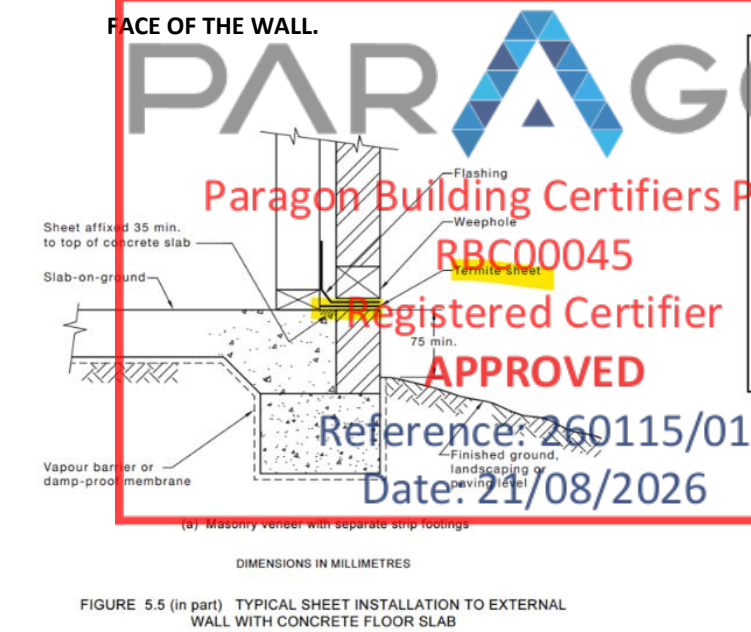


OVERFLOW TO BALCONY:

- SURFACE DRAIN & OVERFLOW TO BALCONY

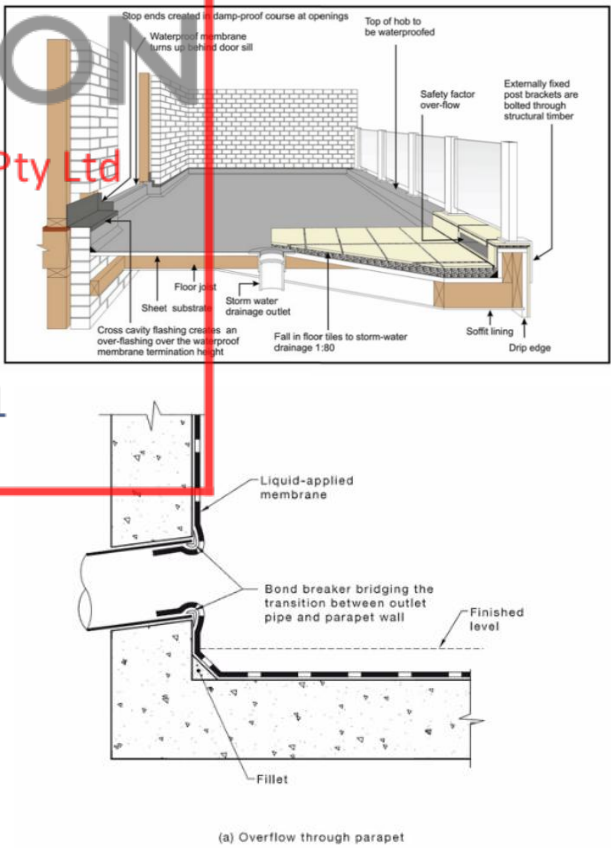

DPC FOR BRICKS

DAMP-PROOF COURSE (DPC) TO EXTENDS THROUGH THE ENTIRE MASONRY LEAF AND NEED TO BE VISIBLE AT THE FINISHED FACE OF THE WALL FROM OUTSIDE

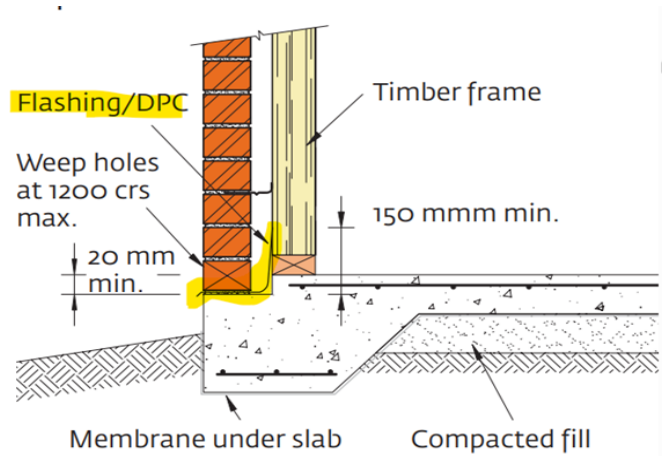

WATERPROOFING

FALL TO FLOOR WASTE TO BE MINIMUM 1:80 TO MAXIMUM 1:50

Figure 10.2.29: Typical membrane termination at drainage outlet



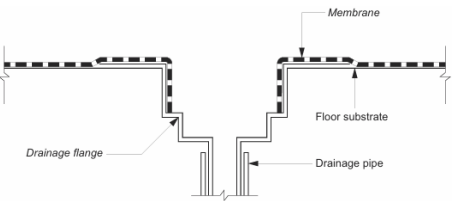


Figure 10.2.24: Typical bathroom door details for whole bathroom waterproofing

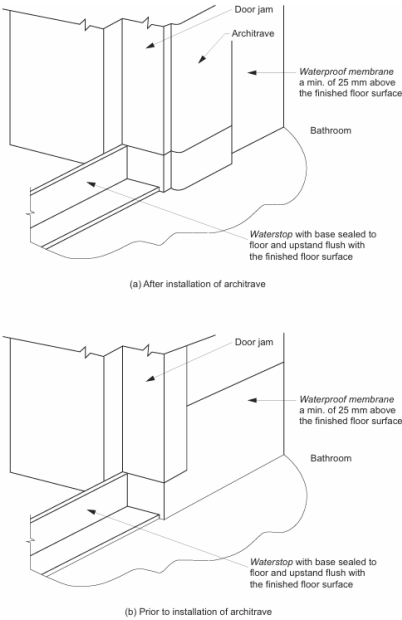


ENCLOSED SHOWER AREA

Figure 10.2.17: Typical hobless construction

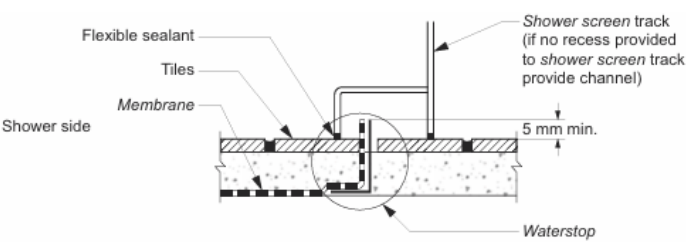


Extent of treatment for shower areas — concrete compressed fibre-cement and fibre-cement sheet floors

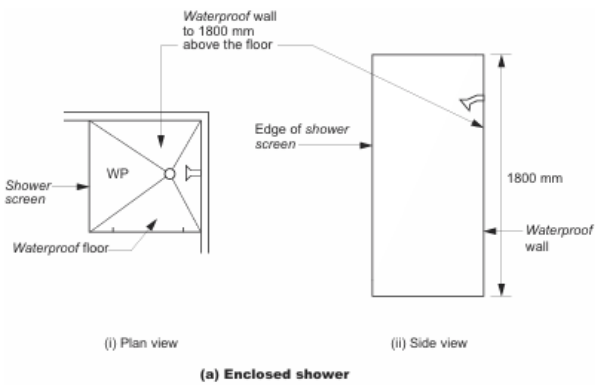

BASIN & BATHTUB

Figure 10.2.5: Bath and vessel abutting wall — areas to be protected

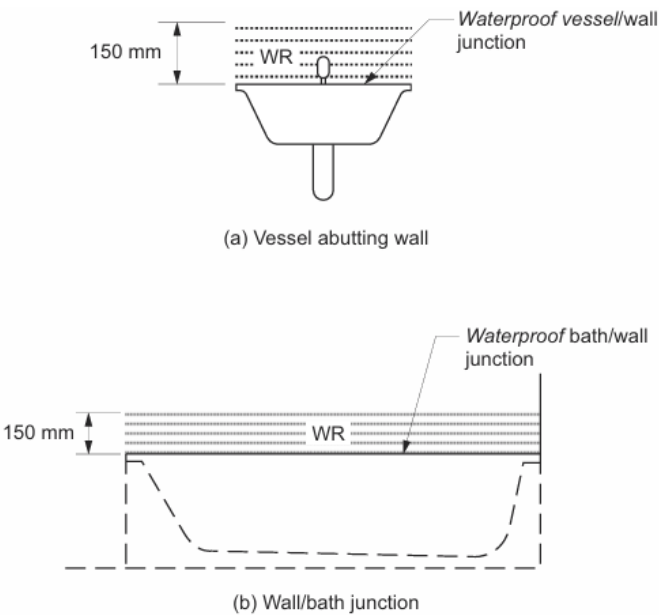


REV	DATE	DESCRIPTION	BY
5	31-07-2026	CC ISSUE	
4	29-06-2026	RFI 3 ISSUE	
3	16-06-2026	RFI 2 ISSUE	
2	26-05-2026	RFI ISSUE	
1	22-04-2026	DA ISSUE	



RUBY
HOMES

THIS DRAWING IS THE EXCLUSIVE PROPERTY OF THE DEVELOPER & THE REPRODUCTION OF ANY PART WITHOUT THE PRIOR WRITTEN CONSENT OF THE DEVELOPER IS A VIOLATION OF APPLICABLE LAWS. IN NO EVENT SHALL THE DEVELOPER BE HELD LIABLE FOR SPECIAL COLLATERAL, INCIDENTAL OR CONSEQUENTIAL LIABILITY IN CONNECTION WITH THE USE OF THIS DIGITAL DATA ONCE RELEASED FROM THE DEVELOPER'S OFFICE. THIS DRAWING IS TO BE READ & UNDERSTOOD IN CONJUNCTION WITH THE STRUCTURAL, MECHANICAL, ELECTRICAL & / OR ANY OTHER CONSULTANT'S DOCUMENTATION AS MAY BE APPLICABLE TO THE PROJECT PRIOR TO THE START OF ANY WORKS AND FOR ITS DURATION.

PROJECT: Residential Dwelling		DRAWING TITLE: GENERAL NOTES		NORTH:		LOT NO: 1008		DATE: 11-08-2026	SCALE: 1 : 2	DRAWING No: CC.02B		REV: 5
LOT 1008 IN DP 1306994 LOCATED AT No.16 Ridgeway Drive Orchard Hills NSW.						DRAWN BY: AS	CHECKED BY: RH					ISSUED BY:
						DRAFTED BY: SL	CLIENT NAME: Saggita Reddy					

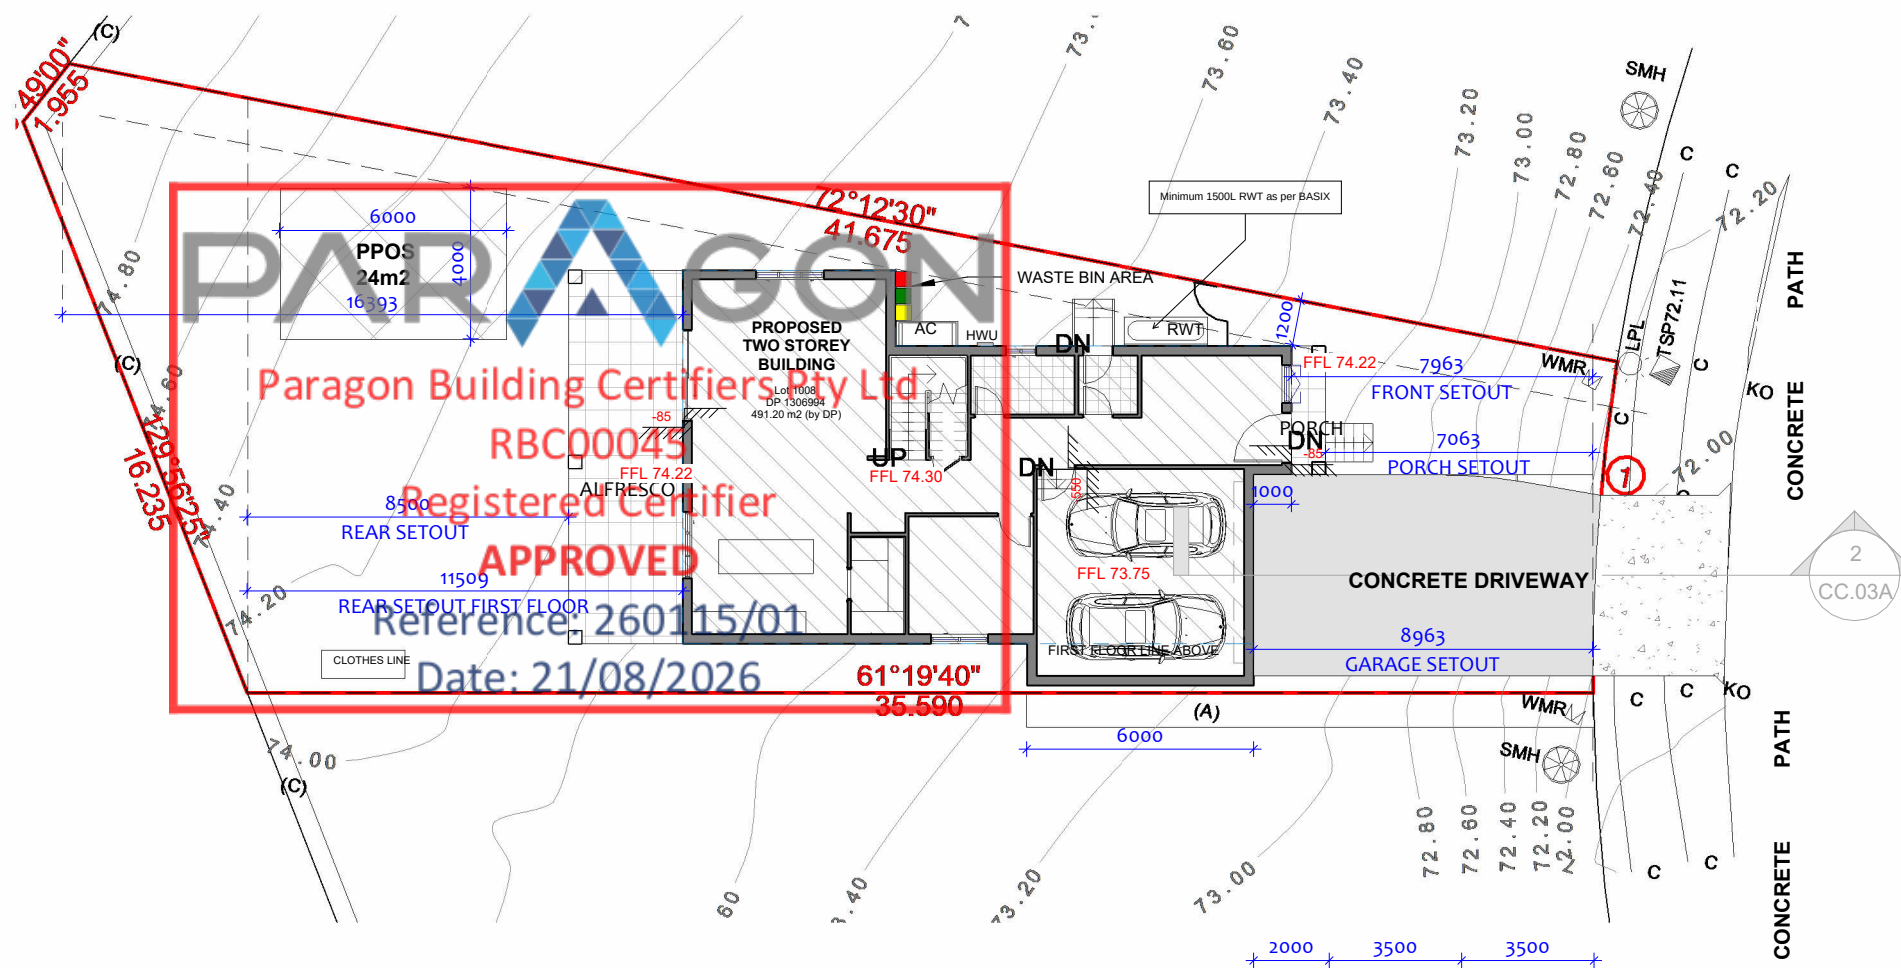

RIDGEWAY DRIVE


HOUSING CODE COMPLIANCE TABLE

DESCRIPTION		COMPLIANCE		COMMENT
ELEMENT	CODE CONTROL	REQUIREMNT	PROPOSED	
LAND ZONE	1 GENERAL RESIDENTIAL			
LOT NO	LOT 1008			
LOT AREA	491.2 m2			
LOT WIDTH	Standard Lot Min. 6m at Building Line facing primary road	6.0m	11.11m	YES
HEIGHT	MAX. Height	9m	8.1m (MAX.)	YES
FRONT SETBACK	FRONT SET BACK (Min. Setback from Primary Road) For 300-350 sqm. Lot	4.5 m	7.963m	YES
REAR SET BACK (MIN.)	GROUND FLOOR	3m	8.5m	YES
	FIRST FLOOR	6m	11.5 m	
SIDE SET BACK (MIN.)	GROUND FLOOR	0/0.9m	0.2/1.2m	YES
	FIRST FLOOR	1.2m	1.5/1.2m	
SITE COVERAGE	GROUND FLOOR	294 m2(60%)	126 m2(25.6%)	YES
	FIRST FLOOR	172 m2(35%)	119 m2(24.2%)	
PRIVATE OPEN SPACE	24m2 minimum area and 4.0m minimum dimension		24 m2	YES
LANDSCAPE AREA	Minimum of 25% of lot area. Minimum of one tree in the front and rear setback. =122.2 m2		240.8m2(49%)	YES

CC - SITE PLAN

1

1 : 200

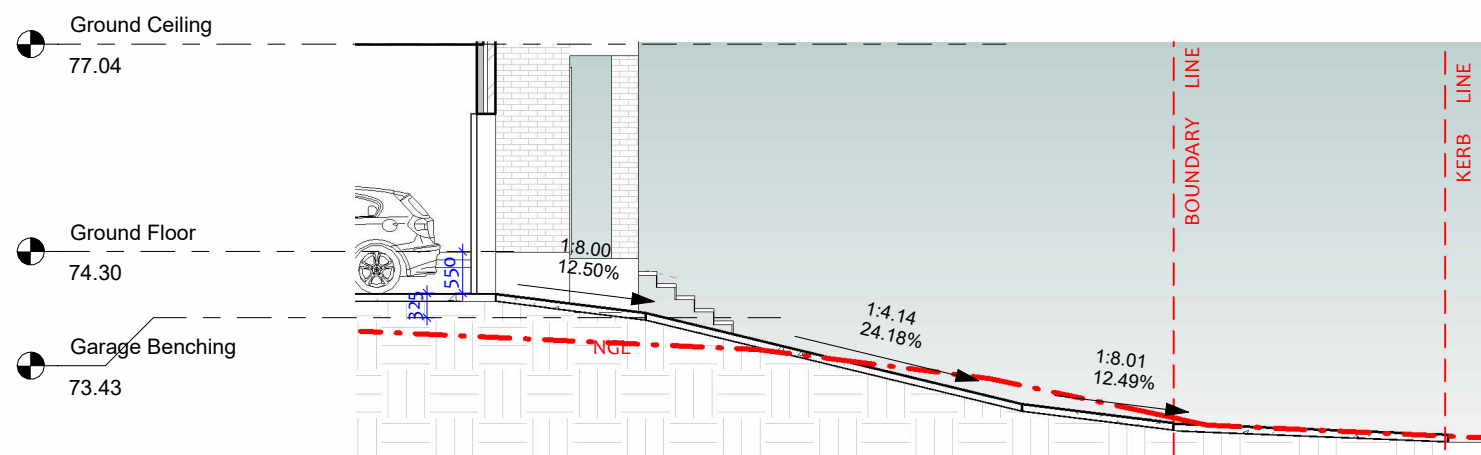

DRIVEWAY SECTION

2

1 : 100

REV	DATE	DESCRIPTION	BY
5	31-07-2026	CC ISSUE	
4	29-06-2026	RFI 3 ISSUE	
3	16-06-2026	RFI 2 ISSUE	
2	26-05-2026	RFI ISSUE	
1	22-04-2026	DA ISSUE	


RUBY HOMES

THIS DRAWING IS THE EXCLUSIVE PROPERTY OF THE DEVELOPER & THE REPRODUCTION OF ANY PART WITHOUT THE PRIOR WRITTEN CONSENT OF THE DEVELOPER IS A VIOLATION OF APPLICABLE LAWS. IN NO EVENT SHALL THE DEVELOPER BE HELD LIABLE FOR SPECIAL COLLATERAL, INCIDENTAL OR CONSEQUENTIAL LIABILITY IN CONNECTION WITH THE USE OF THIS DIGITAL DATA ONCE RELEASED FROM THE DEVELOPER'S OFFICE. THIS DRAWING IS TO BE READ & UNDERSTOOD IN CONJUNCTION WITH THE STRUCTURAL, MECHANICAL, ELECTRICAL & / OR ANY OTHER CONSULTANT'S DOCUMENTATION AS MAY BE APPLICABLE TO THE PROJECT PRIOR TO THE START OF ANY WORKS AND FOR ITS DURATION.

PROJECT:
Residential Dwelling

LOT 1008 IN DP 1306994
LOCATED AT No.16 Ridgeway Drive Orchard Hills NSW.

DRAWING TITLE:
LOCATION PLAN AND SITE PLAN

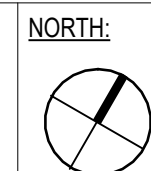

LOT NO:	1008	DATE:	11-08-2026	SCALE:	As indicated	DRAWING No:	CC.03A	REV:	5
DRAWN BY:	AS	CHECKED BY:	RH						
DRAFTED BY:	SL	CLIENT NAME:	Saggita Reddy						

CC ISSUE



Paragon Building Certifiers Pty Ltd


RBC00045

Registered Certifier

APPROVED

Reference: 260115/01

Date: 21/08/2026

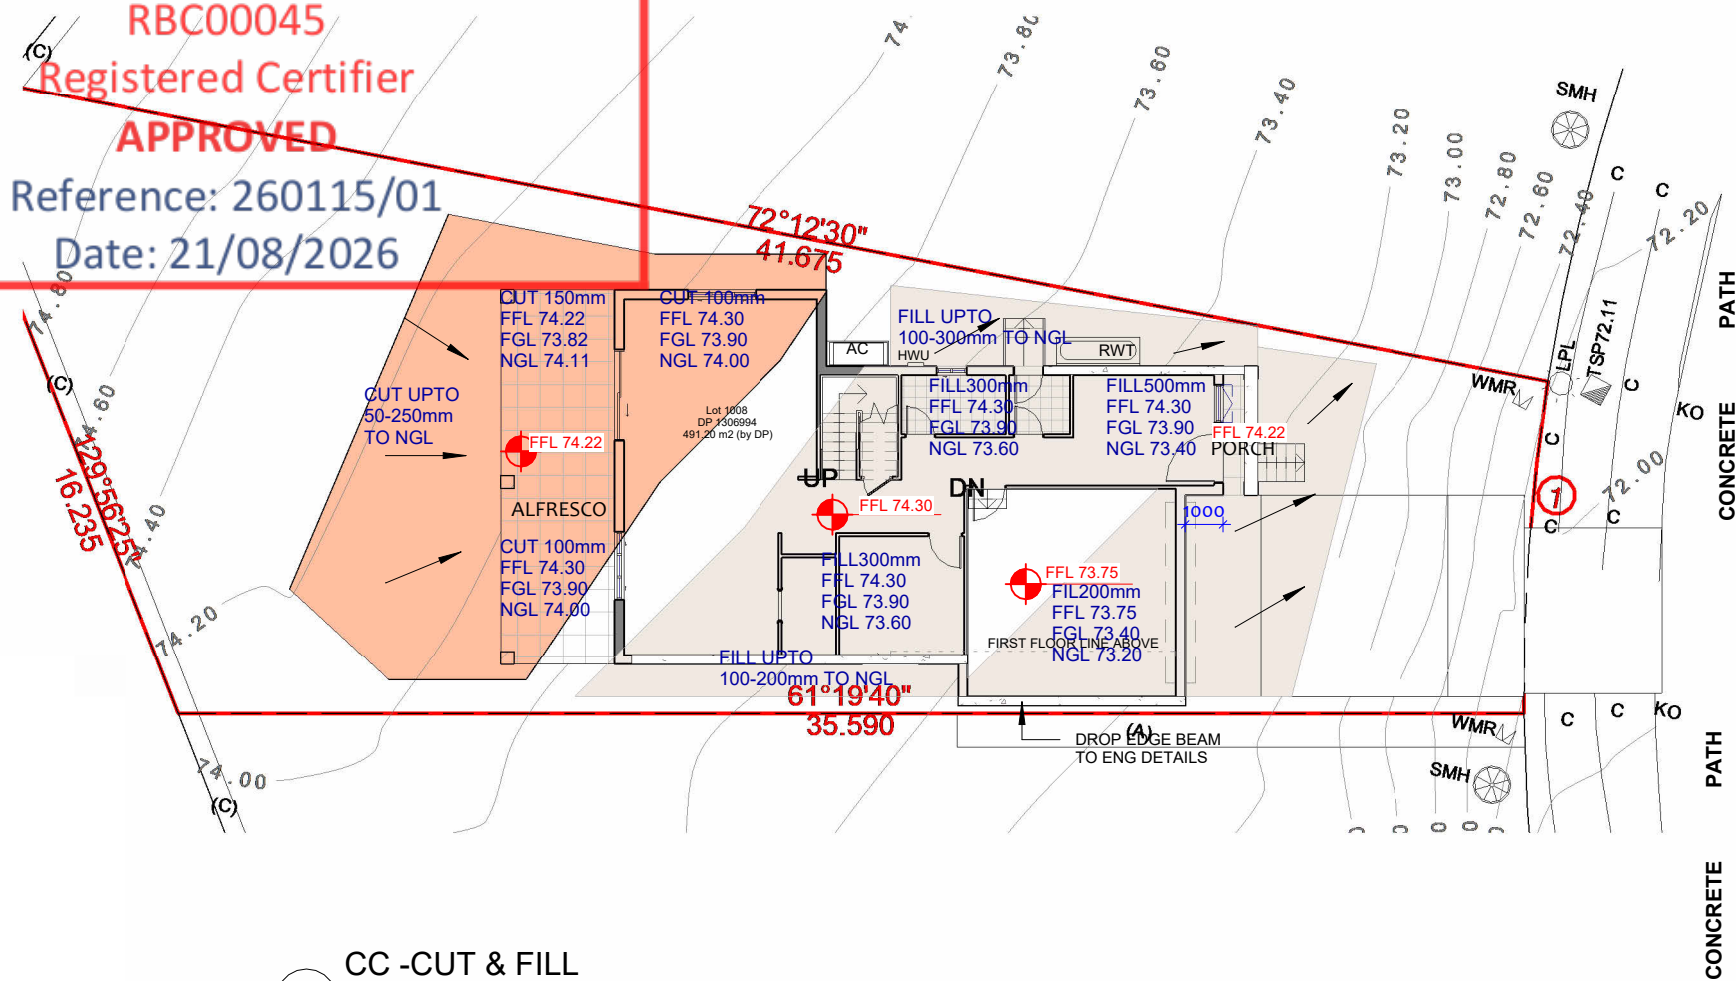

LEGENDS

- CUT UPTO 250MM
- FILL UPTO 250MM
- DROP EDGE BEAM TO RETAIN

1 CC -CUT & FILL
1 : 200


REV	DATE	DESCRIPTION	BY
5	31-07-2026	CC ISSUE	
4	29-06-2026	RFI 3 ISSUE	
3	16-06-2026	RFI 2 ISSUE	
2	26-05-2026	RFI ISSUE	
1	22-04-2026	DA ISSUE	

THIS DRAWING IS THE EXCLUSIVE PROPERTY OF THE DEVELOPER & THE REPRODUCTION OF ANY PART WITHOUT THE PRIOR WRITTEN CONSENT OF THE DEVELOPER IS A VIOLATION OF APPLICABLE LAWS. IN NO EVENT SHALL THE DEVELOPER BE HELD LIABLE FOR SPECIAL COLLATERAL, INCIDENTAL OR CONSEQUENTIAL LIABILITY IN CONNECTION WITH THE USE OF THIS DIGITAL DATA ONCE RELEASED FROM THE DEVELOPER'S OFFICE. THIS DRAWING IS TO BE READ & UNDERSTOOD IN CONJUNCTION WITH THE STRUCTURAL, MECHANICAL, ELECTRICAL & / OR ANY OTHER CONSULTANT'S DOCUMENTATION AS MAY BE APPLICABLE TO THE PROJECT PRIOR TO THE START OF ANY WORKS AND FOR ITS DURATION.


PROJECT:
Residential Dwelling

LOT 1008 IN DP 1306994
LOCATED AT No.16 Ridgeway
Drive Orchard Hills NSW.

DRAWING TITLE:
SITE CUT/FILL

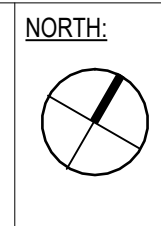





LOT NO:	DATE:	SCALE:	DRAWING No:	REV:
1008	11-08-2026	1 : 200	CC.03B	5
DRAWN BY:	CHECKED BY:			
AS	RH			
DRAFTED BY:	CLIENT NAME:			
SL	Saggita Reddy			

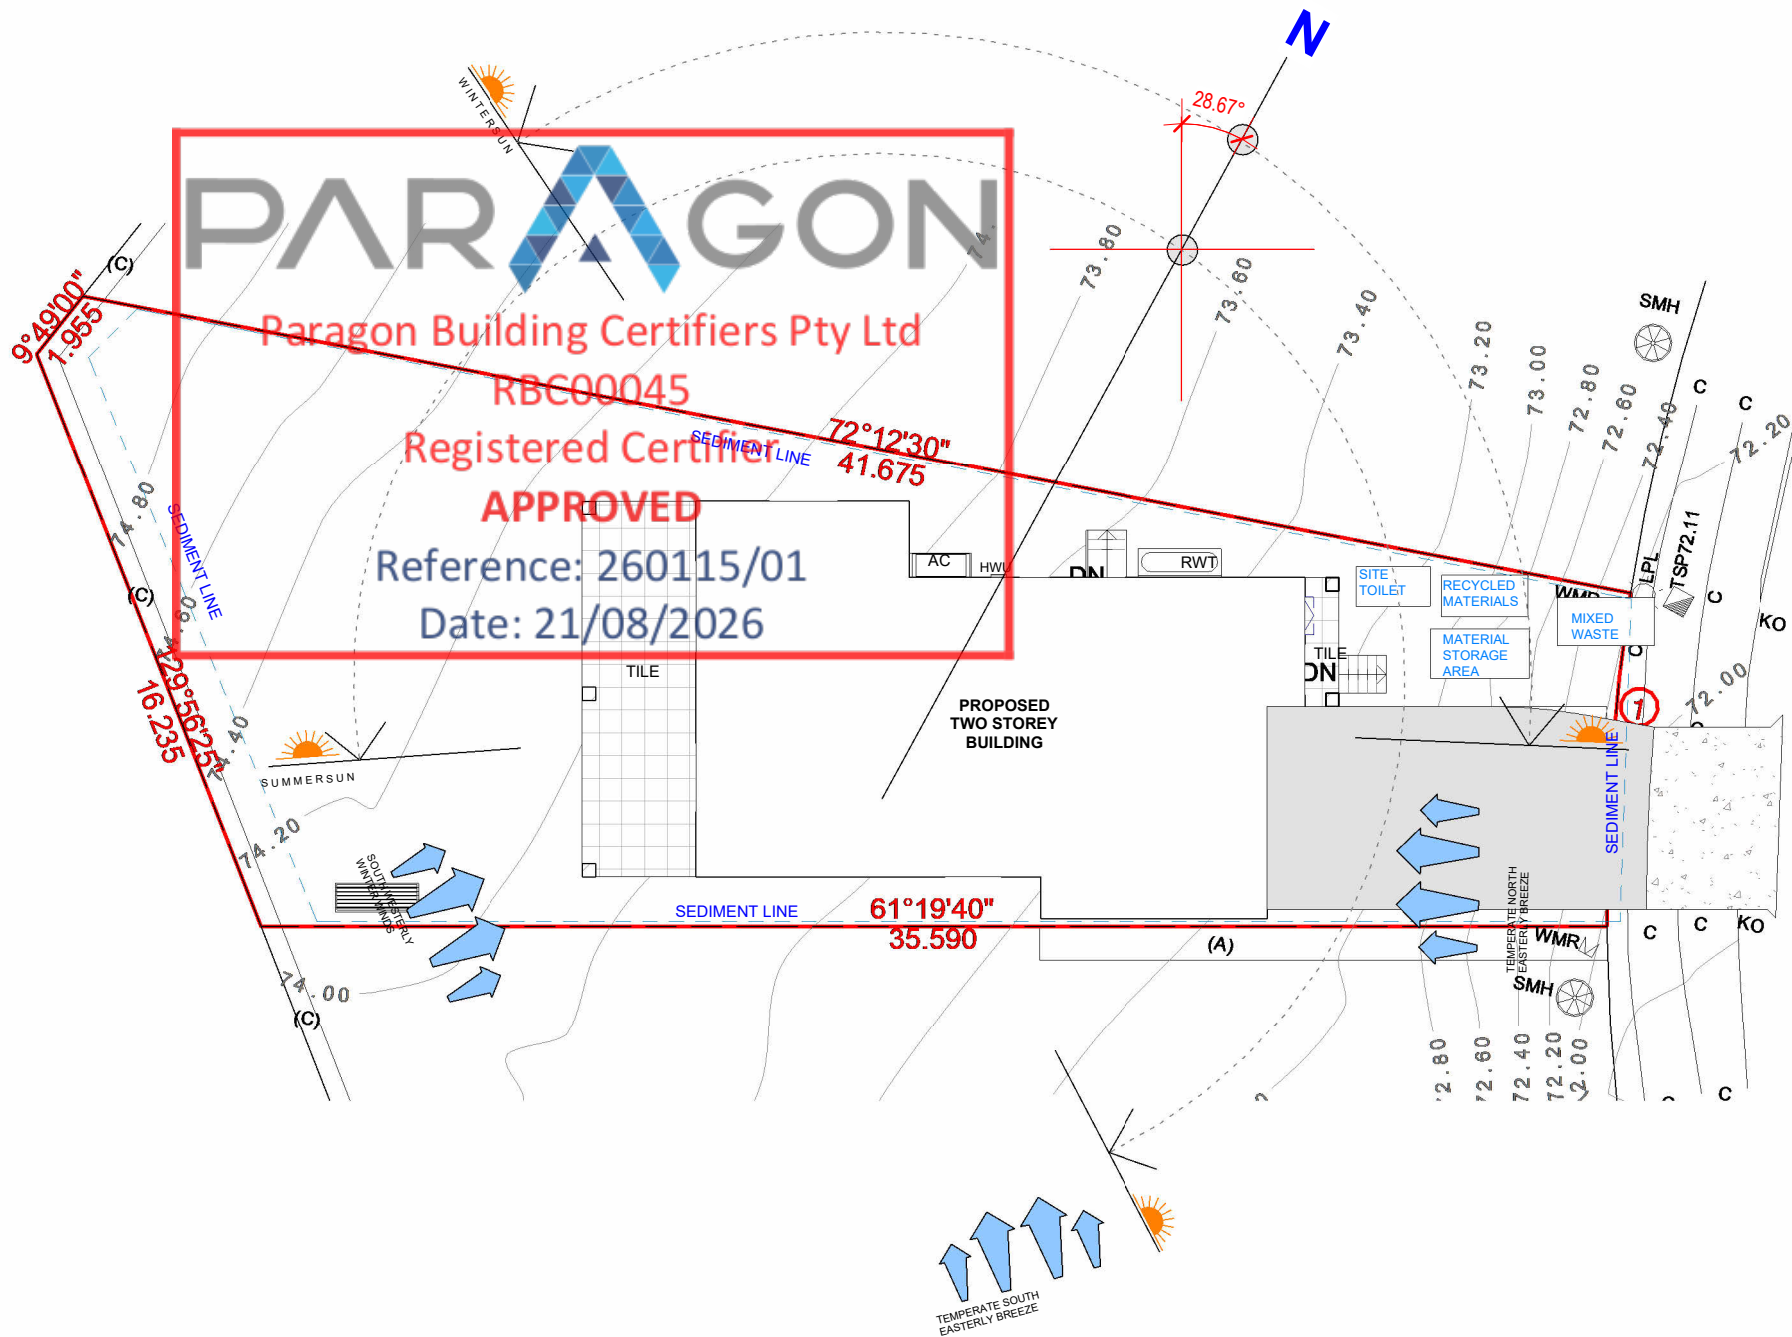

RIDGEWAY DRIVE

SITE ANALYSIS AND SEDIMENT CONTROL PLAN

1
1 : 200

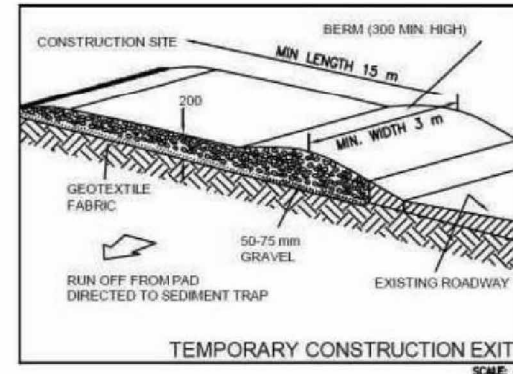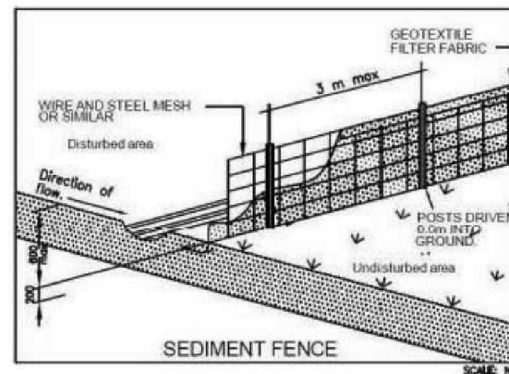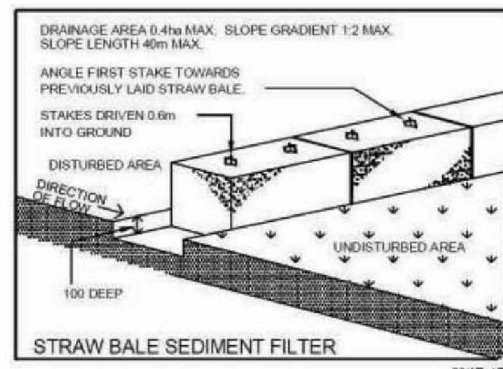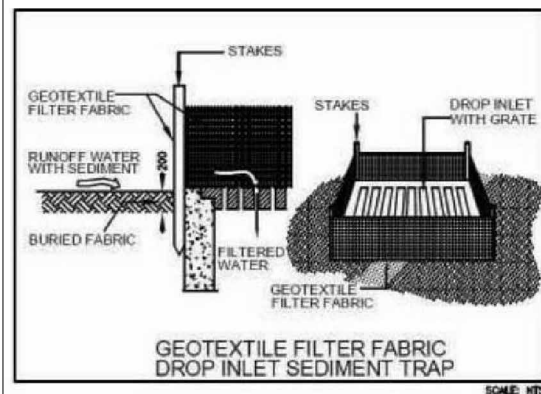

- SEDIMENT AND EROSION NOTES:**
- THIS PLAN TO BE READ IN CONJUNCTION WITH SEDIMENT AND EROSION CONTROL DETAILS AS ATTACHED.
 - THE CONTRACTOR SHALL IMPLEMENT ALL SOIL EROSION AND SEDIMENT CONTROL MEASURES AS NECESSARY AND TO THE SATISFACTION OF COUNCIL PRIOR TO THE COMMENCEMENT AND DURING CONSTRUCTION. NO DISTURBANCE TO THE SITE SHALL BE PERMITTED OTHER THAN IN THE IMMEDIATE AREA OF THE WORK AND NO MATERIAL SHALL BE REMOVED FROM THE SITE WITHOUT COUNCIL'S APPROVAL. ALL SEDIMENT AND EROSION CONTROL DEVICES TO BE INSTALLED AND MAINTAINED IN ACCORDANCE WITH STANDARDS OUTLINED IN NSW DEPARTMENT OF HOUSING "MANAGING URBAN STORMWATER-SOILS AND CONSTRUCTIONS". TOPSOIL SHALL BE STRIPPED AND STOCKPILED OUTSIDE HAZARDOUS AREAS SUCH AS DRAINAGE LINES. THIS TOP SOIL IS TO BE RESPIRED LATER ON AREAS TO BE REVEGETATED AND STABILISED ONLY. (I.E ALL FOOTPATHS, BATTERS, SITE REGARDING AREAS, BASINS AND CATCH DRAINS), TOPSOIL SHALL NOT BE RESPIRED ON ANY OTHER AREAS UNLESS SPECIALLY INSTRUCTED BY THE SUPERINTENDENT. IF THEY ARE TO REMAIN FOR LONGER THAN ONE MONTH STOCKPILES SHALL BE PROTECTED FROM EROSION BY COVERING THEM WITH A MULCH AND HYDROSEEDING AND, IF NECESSARY, BY LOCATING BANKS OR DRAINS DOWNSTREAM OF A STOCKPILE TO RETARD SILT LADEN RUNOFF.
 - THE CONTRACTOR SHALL REGULARLY MAINTAIN ALL SEDIMENT AND EROSION CONTROL DEVICES AND REMOVE ACCUMULATED SILT FROM SUCH DEVICES SUCH THAT MORE THAN 60% OF THEIR CAPACITY LOST. ALL THE SILTS TO BE PLACED OUTSIDE THE LIMIT OF WORKS. THE PERIOD FOR MAINTAINING THESE DEVICES SHALL BE AT LEAST UNTIL ALL DISTURBED AREAS ARE REVEGETATED AND FURTHER AS MAY BE DIRECTED BY THE SUPERINTENDENT OR COUNCIL.
 - LAY TURF STRIP (MIN 300 mm WIDE) ON 100 mm TOPSOIL WITH 1.0 m LONG RETURNS EVERY 6.0m BEHIND ALL KERB AT THE TOP OF ALL BATTERS AND AROUND STRUCTURES IMMEDIATELY AFTER BACKFILLING OR FORMATION.
 - THE CONTRACTOR SHALL GRASS SEED ALL DISTURBED AREAS WITH AN APPROVED MIX AS SSON AS PRACTICABLE AFTER COMPLETION OF EARTHWORKS AND REGRADING.
 - VEHICULAR TRAFFIC SHALL BE CONTROLLED DURING CONSTRUCTION CONFINING ACCESS WHERE POSSIBLE TO NOMINATED STABILISED ACCESS POINTS.
 - WHEN ANY DEVICES ARE TO BE HANDED OVER TO COUNCIL, THEY SHALL BE IN CLEAN AND STABLE CONDITION.
 - THE CONTRACTOR SHALL IMPLEMENT DUST CONTROL BY REGULAR WETTING DOWN (BUT NOT SATURATING) DISTURBED AREA.
 - PROVIDE AND MAINTAIN SILT TRAPS AROUND ALL SURFACE INLET PITS UNTIL CATCHMENT IS REVEGETATED OR PAVED.
 - REVEGETATE ALL TRENCHES IMMEDIATELY UPON COMPLETION OF BACKFILLING.
 - ALL DRAINAGE PIPE INLETS TO BE CAPPED UNTIL:
 - A) DOWNPIPES CONNECTED
 - B) PITS CONSTRUCTED & PROTECTED WITH SILT BARRIER

SITE WORKS NOTES

- ORIGIN OF LEVELS PROVIDED BY SURVEYOR
- THE BUILDER SHALL VERIFY ALL DIMENSIONS AND EXISTING LEVELS ON SITE PRIOR TO THE COMMENCEMENT OF WORK AND ANY DISCREPANCIES SHALL BE REPORTED TO THE SURVEYOR / ENGINEER.
- TOPSOIL SHALL BE STRIPPED FROM THE CONSTRUCTION AREA AND STOCKPILED ON SITE, TO BE LATER SPREAD OR DISPOSED OFF SITE, AS DIRECTED BY SUPERVISOR / ENGINEER.
- ALL TRENCH BACKFILL MATERIAL SHALL BE COMPACTED TO THE SAME DENSITY AS THE ADJACENT MATERIAL.
- ALL SERVICE TRENCHES UNDER VEHICULAR PAVEMENTS SHALL BE BACKFILLED WITH SAND OR APPROVED GRANULAR MATERIALS, TO THE UNDERSIDE OF THE PAVEMENT, AND COMPACTED TO 98% STANDARD MAXIMUM DRY DENSITY, IN ACCORDANCE WITH AS 1289E1.1.

TEMPORARY 1.8M HIGH WIRE MESH FENCE WITH DUSTPROOF MESH APPLIED TO FULL HEIGHT TO BOUNDARIES AS REQUIRED

LOCATION OF WASTE BINS
SEDIMENT FENCE AS REQUIRED
GRAVEL ACCESS
SITE ACCESS AREA TO BE USED FOR WASHDOWN AREA
FOOTPATH CLEAN AND CLEAR AT ALL TIMES

SD 5-7 STABILISED SITE ACCESS

- STRIP TOPSOIL AND LEVEL SITE.
- COMPACT SUBGRADE.
- COVER AREA WITH GEOTEXTILE.
- CONSTRUCT 200 mm THICK PAD OVER GEOTEXTILE USING ROADBASE OR 30 mm AGGREGATE. Min 15 m LONG OR TO BUILDING ALIGNMENT. Min 3 m WIDE.
- CONSTRUCT HUMP IMMEDIATELY WITHIN BOUNDARY TO DIVERT WATER TO A SEDIMENT FENCE OR OTHER SEDIMENT TRAP.

LOCATION OF STOCKPILE MATERIAL
MATERIAL STORAGE AREA
TEMPORARY TOILETS
INSTALL TEMPORARY SEDIMENT BARRIERS TO ALL INLET PITS LIKELY TO COLLECT SILT LADEN WATER, TO COUNCIL'S REQUIREMENTS.

SD 6-9 GEOTEXTILE INLET FILTER

- FABRICATE A SEDIMENT BARRIER MADE FROM GEOTEXTILE. REFER SD6-7 FOR DETAILS.
- SUPPORT GEOTEXTILE WITH MESH TIED TO POSTS AT 1m Ctrs.
- DO NOT COVER INLET WITH GEOTEXTILE.

CC ISSUE

REV	DATE	DESCRIPTION	BY
5	31-07-2026	CC ISSUE	
4	29-06-2026	RFI 3 ISSUE	
3	16-06-2026	RFI 2 ISSUE	
2	26-05-2026	RFI ISSUE	
1	22-04-2026	DA ISSUE	

RUBY HOMES


THIS DRAWING IS THE EXCLUSIVE PROPERTY OF THE DEVELOPER & THE REPRODUCTION OF ANY PART WITHOUT THE PRIOR WRITTEN CONSENT OF THE DEVELOPER IS A VIOLATION OF APPLICABLE LAWS. IN NO EVENT SHALL THE DEVELOPER BE HELD LIABLE FOR SPECIAL COLLATERAL, INCIDENTAL OR CONSEQUENTIAL LIABILITY IN CONNECTION WITH THE USE OF THIS DIGITAL DATA ONCE RELEASED FROM THE DEVELOPER'S OFFICE. THIS DRAWING IS TO BE READ & UNDERSTOOD IN CONJUNCTION WITH THE STRUCTURAL, MECHANICAL, ELECTRICAL & / OR ANY OTHER CONSULTANT'S DOCUMENTATION AS MAY BE APPLICABLE TO THE PROJECT PRIOR TO THE START OF ANY WORKS AND FOR ITS DURATION.

PROJECT:
Residential Dwelling

LOT 1008 IN DP 1306994
LOCATED AT No.16 Ridgeway Drive Orchard Hills NSW.

DRAWING TITLE:

SITE ANALYSIS AND SEDIMENT CONTROL

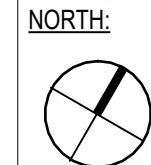


LOT NO:	DATE:	SCALE:	DRAWING No:	REV:
1008	11-08-2026	As indicated	CC.04	5
DRAWN BY:	CHECKED BY:	CLIENT NAME:	ISSUED BY:	
AS	RH	Saggita Reddy		
DRAFTED BY:	SL			

☒ BAL LOW


Waterproofing work to be as per Part 10.2 of the ABCB Housing Provisions Standard 2022

IMPORTANT NOTES:
ALL DIMENSIONS AND NOTES ON ALL PLANS MUST BE CHECKED AND VERIFIED BY BUILDERS AND OWNER PRIOR TO COMMENCEMENT OF ANY BUILDING WORKS. TO CLARIFY AND CONFIRM WITH CONSTRUCTION COMPANY FOR DISCREPANCIES ON ALL DOCUMENTS AND PLANS PROVIDED FOR CONSTRUCTION. ANY WORK INDICATED ON THE PLAN BUT NOT IN THE SPECIFICATION BUT WHICH IS NECESSARY AS PART OF THE CONTRACT, VARIATION TO PLANS. SPECIFICATIONS MAY NOT BE MADE WITHOUT THE WRITTEN CONSENT OF OWNER. IT IS THE RESPONSIBILITY OF THE BUILDER/END USER TO VERIFY PLANS AND SPECIFICATIONS AS TO THEIR ACCURACY AND COMPLY CURRENT BCA AND AUSTRALIAN STANDARDS. WINDOWS TO COMPLY WITH 3.9.3.5 OF THE BCA.

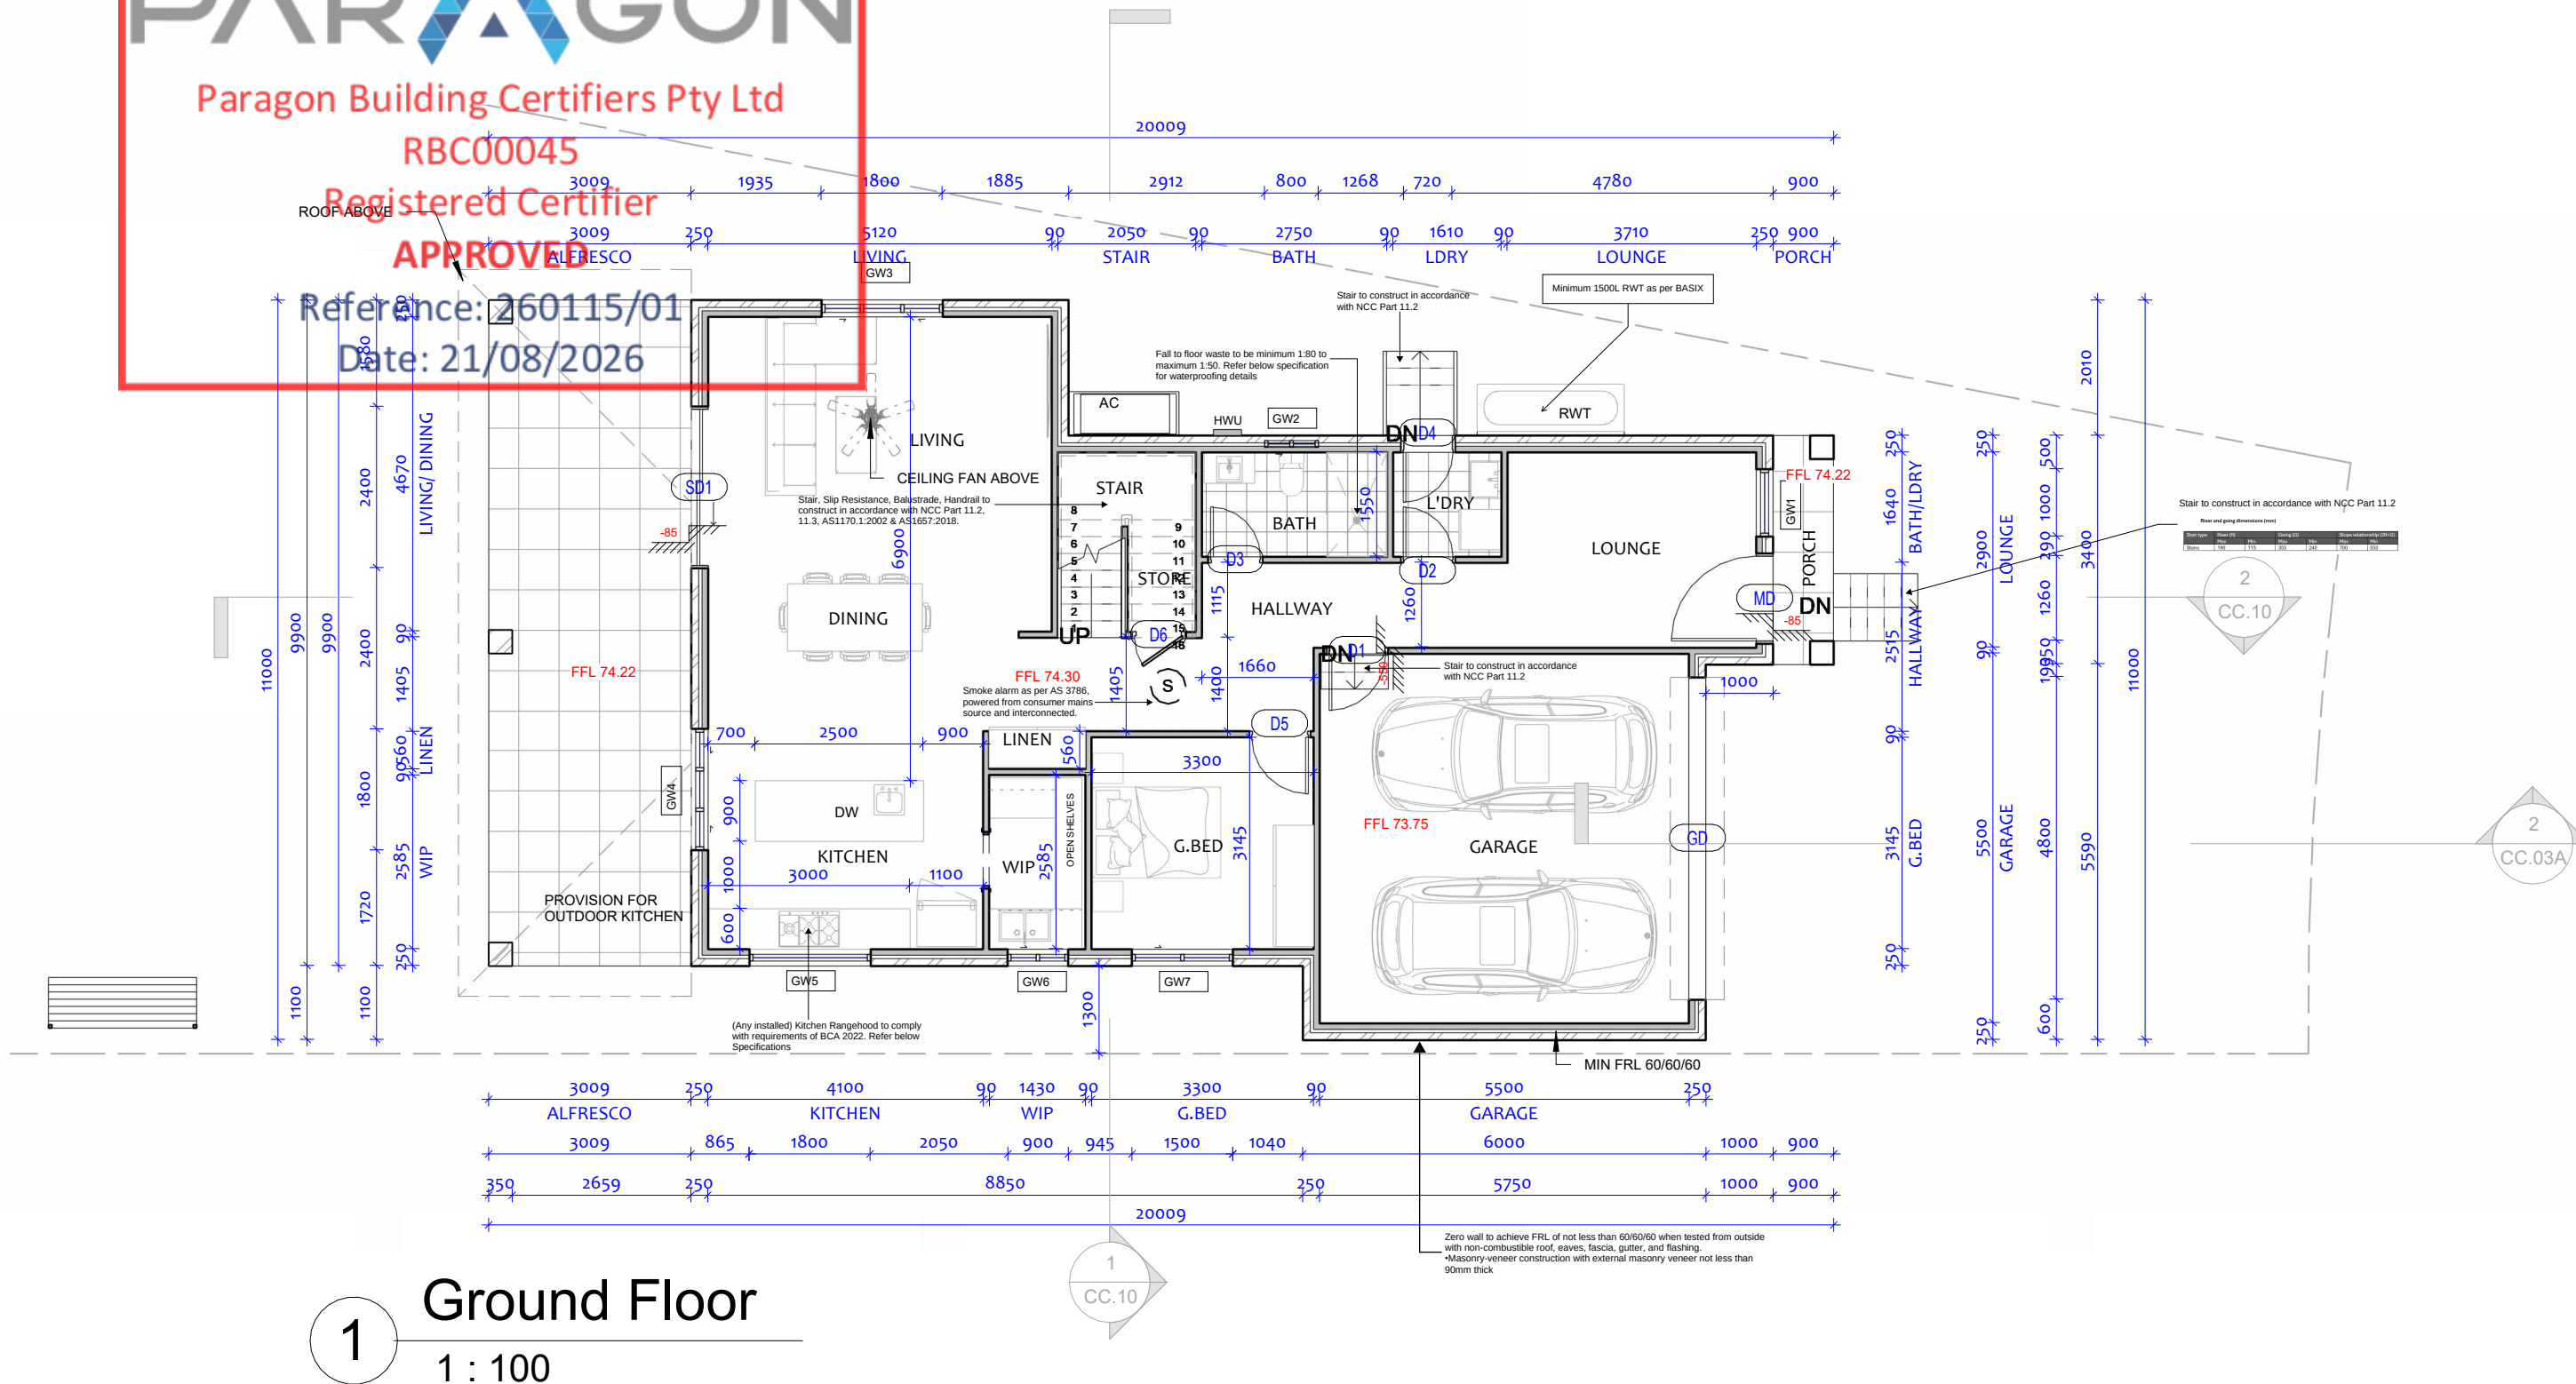

NOTE: PLEASE REFER TO TENDER FOR ALL INCLUSIONS.

5	31-07-2026	CC ISSUE	
4	29-06-2026	RFI 3 ISSUE	
3	16-06-2026	RFI 2 ISSUE	
2	26-05-2026	RFI ISSUE	
1	22-04-2026	DA ISSUE	
REV	DATE	DESCRIPTION	BY

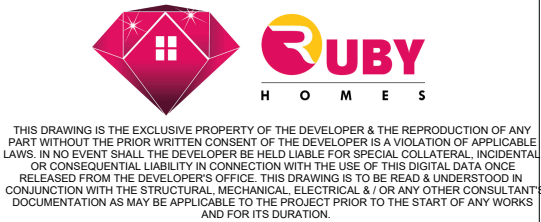

PROJECT:
Residential Dwelling
LOT 1008 IN DP 1306994
LOCATED AT No.16 Ridgeway
Drive Orchard Hills NSW.

DRAWING TITLE:

**GROUND FLOOR
PLAN**



		CC ISSUE		
LOT NO:	DATE:	SCALE:	<u>DRAWING No:</u>	<u>REV:</u>
1008	11-08-2026	1 : 100	CC.05	5
DRAWN BY:	CHECKED BY:			ISSUED BY:
AS	RH			
DRAFTED BY:	CLIENT NAME:			
SL	Saggita Reddy			

☒ BAL LOW

Waterproofing work to be as per Part 10.2 of the ABCB Housing Provisions Standard 2022

IMPORTANT NOTES:
ALL DIMENSIONS AND NOTES ON ALL PLANS MUST BE CHECKED AND VERIFIED BY BUILDERS AND OWNER PRIOR TO COMMENCEMENT OF ANY BUILDING WORKS. TO CLARIFY AND CONFIRM WITH CONSTRUCTION COMPANY FOR DISCREPANCIES ON ALL DOCUMENTS AND PLANS PROVIDED FOR CONSTRUCTION. ANY WORK INDICATED ON THE PLAN BUT NOT IN THE SPECIFICATION BUT WHICH IS NECESSARY AS PART OF THE CONTRACT, VARIATION TO PLANS, SPECIFICATIONS MAY NOT BE MADE WITHOUT THE WRITTEN CONSENT OF OWNER. IT IS THE RESPONSIBILITY OF THE BUILDER/END USER TO VERIFY PLANS AND SPECIFICATIONS AS TO THEIR ACCURACY AND COMPLY CURRENT BCA AND AUSTRALIAN STANDARDS. WINDOWS TO COMPLY WITH 3.9.3.5 OF THE BCA.

PARAGON

Paragon Building Certifiers Pty Ltd


RBC00045

Registered Certifier

APPROVED

Reference: 260115/01

Date: 21/08/2026

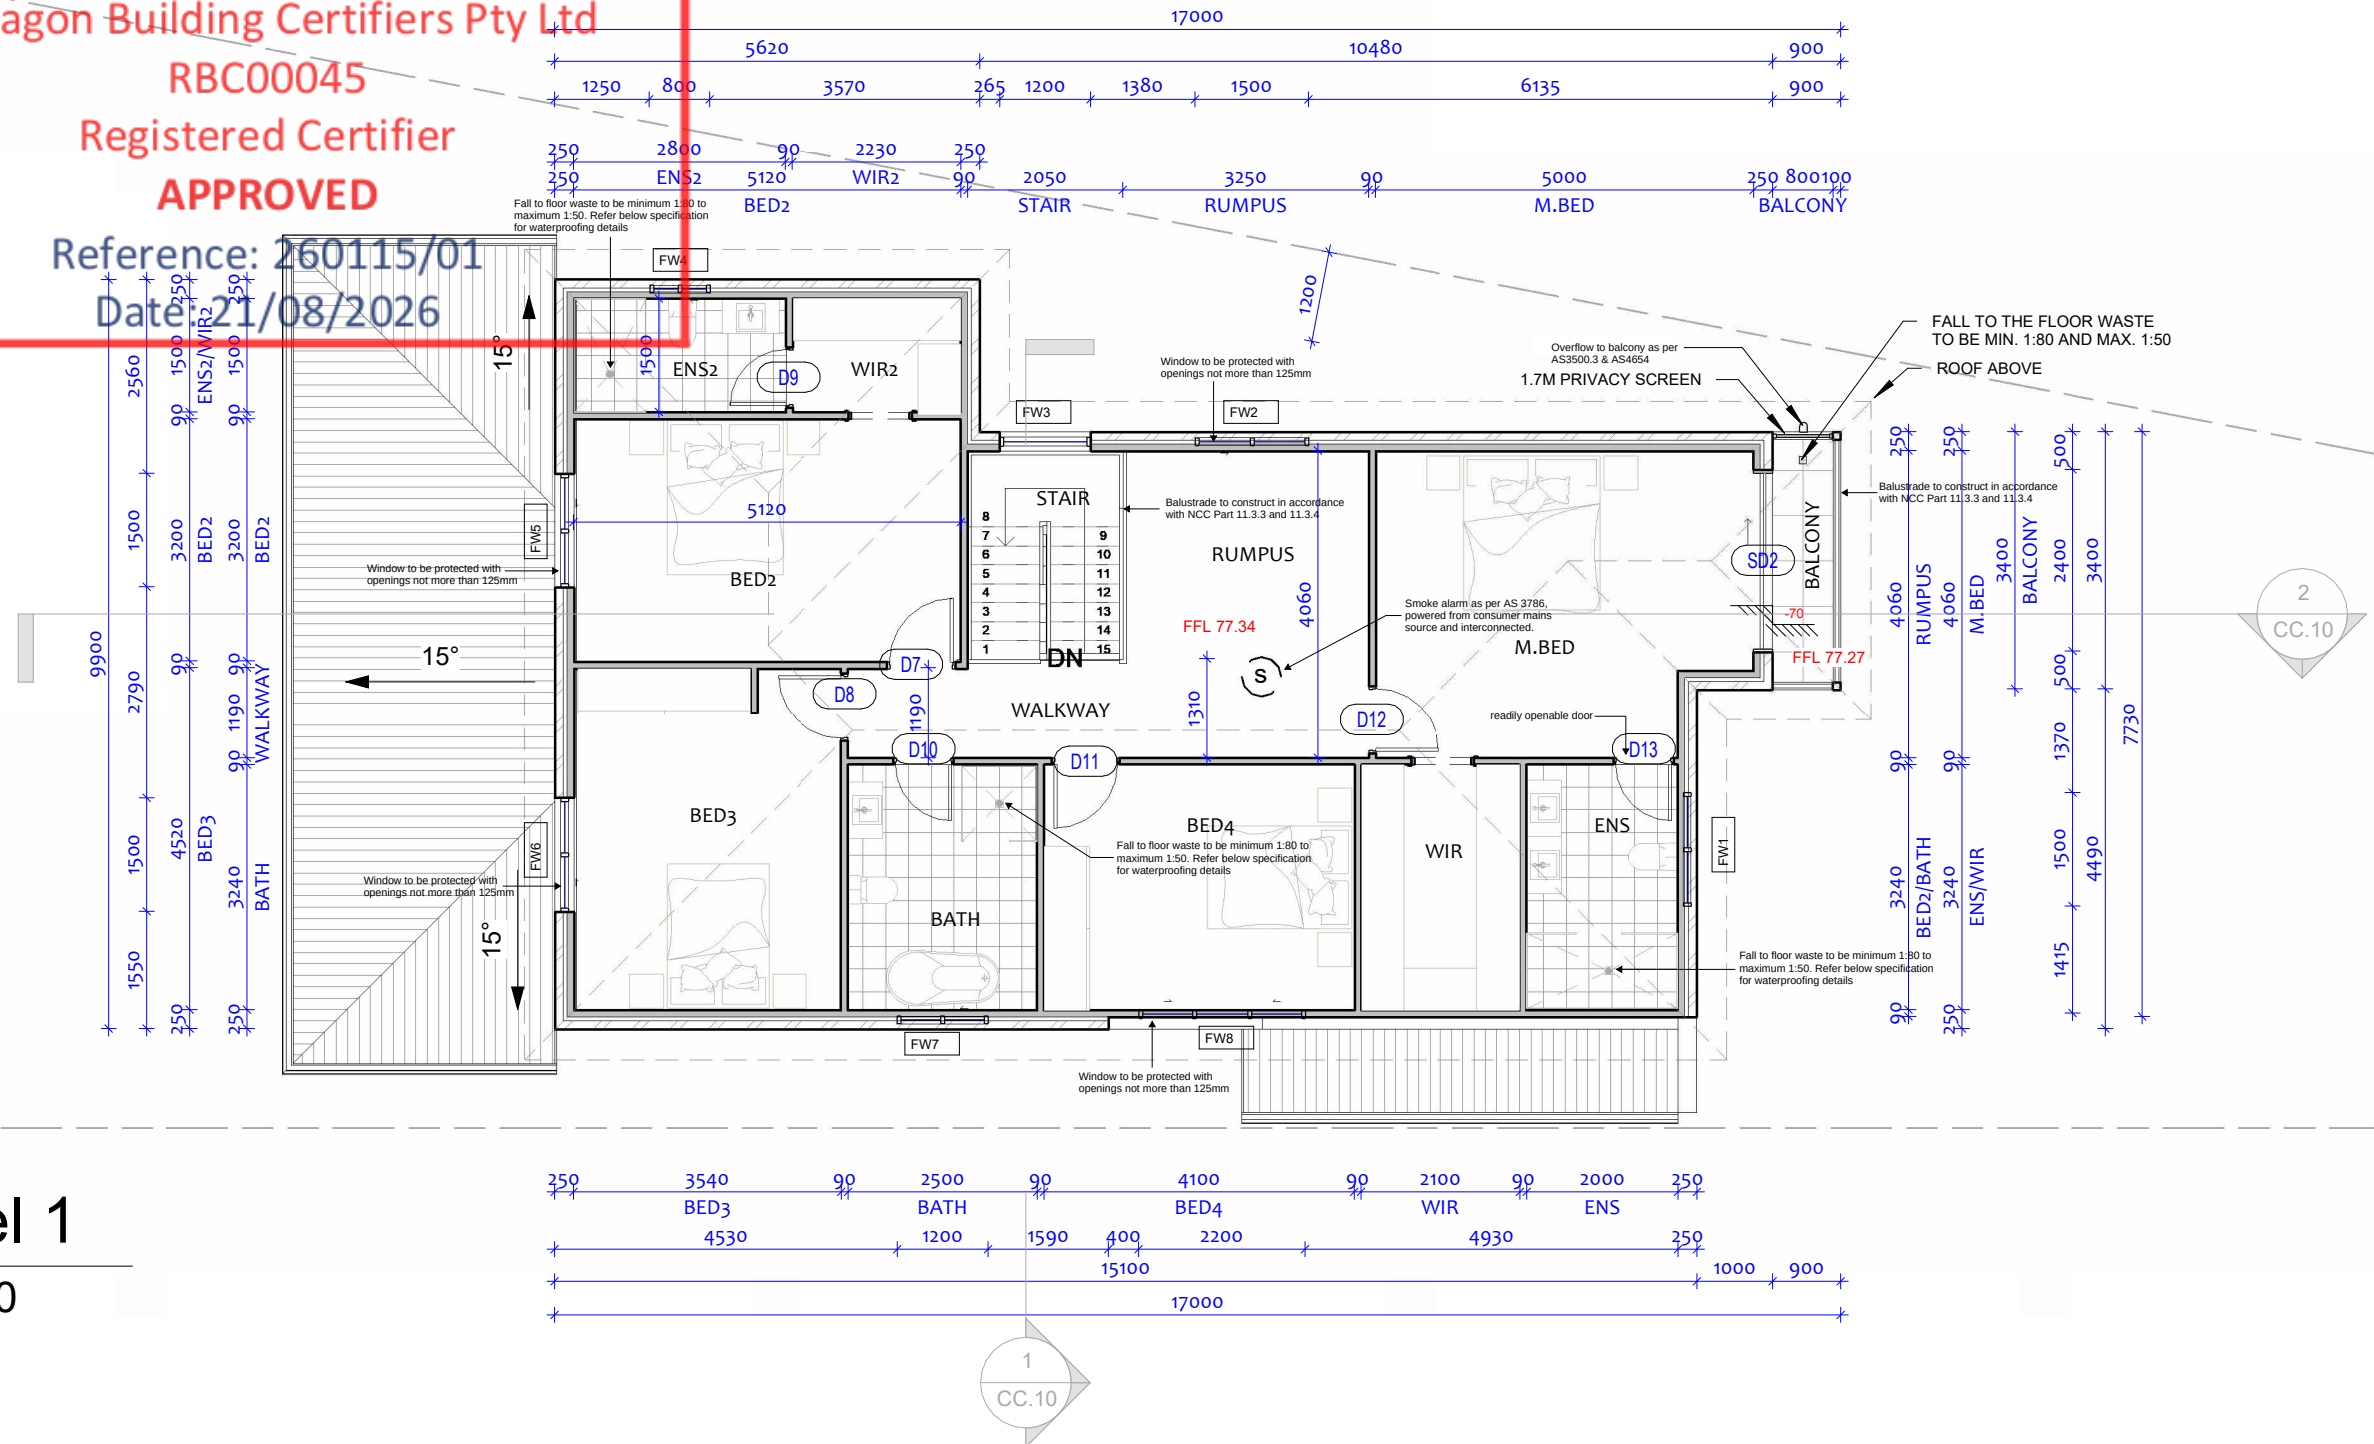

1

Level 1

1 : 100

NOTE: PLEASE REFER TO TENDER FOR ALL INCLUSIONS.


REV	DATE	DESCRIPTION	BY
5	31-07-2026	CC ISSUE	
4	29-06-2026	RFI 3 ISSUE	
3	16-06-2026	RFI 2 ISSUE	
2	26-05-2026	RFI ISSUE	
1	22-04-2026	DA ISSUE	

RUBY HOMES

THIS DRAWING IS THE EXCLUSIVE PROPERTY OF THE DEVELOPER & THE REPRODUCTION OF ANY PART WITHOUT THE PRIOR WRITTEN CONSENT OF THE DEVELOPER IS A VIOLATION OF APPLICABLE LAWS. IN NO EVENT SHALL THE DEVELOPER BE HELD LIABLE FOR SPECIAL COLLATERAL, INCIDENTAL OR CONSEQUENTIAL LIABILITY IN CONNECTION WITH THE USE OF THIS DIGITAL DATA ONCE RELEASED FROM THE DEVELOPER'S OFFICE. THIS DRAWING IS TO BE READ & UNDERSTOOD IN CONJUNCTION WITH THE STRUCTURAL, MECHANICAL, ELECTRICAL & / OR ANY OTHER CONSULTANT'S DOCUMENTATION AS MAY BE APPLICABLE TO THE PROJECT PRIOR TO THE START OF ANY WORKS AND FOR ITS DURATION.

PROJECT:
Residential Dwelling
LOT 1008 IN DP 1306994
LOCATED AT No.16 Ridgeway Drive Orchard Hills NSW.

DRAWING TITLE:
FIRST FLOOR LEVEL

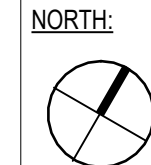

LOT NO:	DATE:	SCALE:	DRAWING No:	REV:
1008	11-08-2026	1 : 100	CC.06	5
DRAWN BY:	CHECKED BY:	DRAFTED BY:	CLIENT NAME:	ISSUED BY:
AS	RH	SL	Saggita Reddy	

☒ BAL LOW

IMPORTANT NOTES:
ALL DIMENSIONS AND NOTES ON ALL PLANS MUST BE CHECKED AND VERIFIED BY BUILDERS AND OWNER PRIOR TO COMMENCEMENT OF ANY BUILDING WORKS. TO CLARIFY AND CONFIRM WITH CONSTRUCTION COMPANY FOR DISCREPANCIES ON ALL DOCUMENTS AND PLANS PROVIDED FOR CONSTRUCTION. ANY WORK INDICATED ON THE PLAN BUT NOT IN THE SPECIFICATION BUT WHICH IS NECESSARY AS PART OF THE CONTRACT, VARIATION TO PLANS, SPECIFICATIONS MAY NOT BE MADE WITHOUT THE WRITTEN CONSENT OF OWNER. IT IS THE RESPONSIBILITY OF THE BUILDER/END USER TO VERIFY PLANS AND SPECIFICATIONS AS TO THEIR ACCURACY AND COMPLY CURRENT BCA AND AUSTRALIAN STANDARDS. WINDOWS TO COMPLY WITH 3.9.3.5 OF THE BCA.

ABCB HOUSING PROVISIONS STANDARD 2022

10.8.3 VENTILATION OF ROOF SPACES

1. IN CLIMATE ZONES 6,7 AND 8, A ROOF MUST HAVE A ROOF SPACE THAT
- (A) IS LOCATED
- (I) IMMEDIATELY ABOVE THE *PRIMARY INSULATION LAYER*, OR
- (II) IMMEDIATELY ABOVE SARKING WITH A *VAPOUR PERMEANCE* OF NOT LESS THAN 1.14 $\mu\text{G/N.S}$, WHICH IS IMMEDIATELY ABOVE THE *PRIMARY INSULATION LAYER* OR
- (III) IMMEDIATELY ABOVE CEILING INSULATION THAT MEETS THE REQUIREMENTS OF 13.2.3(3) AND 13.2.3(4); AND
- (B) HAS A HEIGHT OF NOT LESS THAN 20MM; AND
- (C) IS EITHER -
- (I) VENTILATED TO OUTDOOR AIR THROUGH EVENLY DISTRIBUTED OPENINGS IN ACCORDANCE WITH TABLE 10.8.3; OR
- (II) LOCATED IMMEDIATELY UNDERNEATH THE ROOF TILES OF A UNSARKED TILED ROOF.

Table 10.8.3: Roof space ventilation requirements

Roof pitch	Ventilation openings
< 10°	25,000 mm ² /m provided at each of two opposing ends
≥ 10° and < 15°	25,000 mm ² /m provided at the eaves and 5,000 mm ² /m at high level
≥ 15° and < 75°	7,000 mm ² /m provided at the eaves and 5,000 mm ² /m at high level, plus an additional 18,000 mm ² /m at the eaves if the roof has a cathedral ceiling

Figure 10.8.3 (explanatory): Example of roof space with low level ventilation

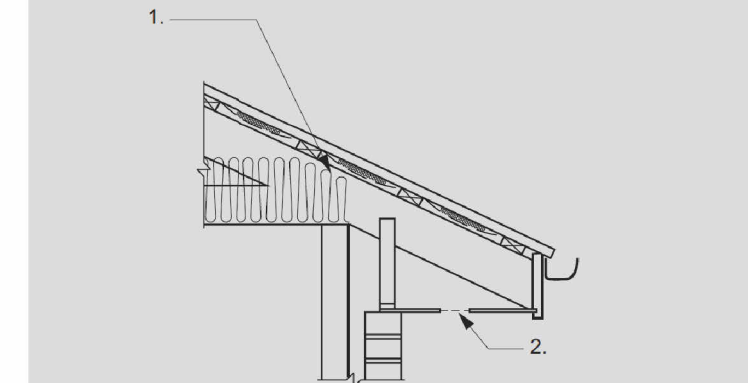




Figure Notes

- (1) Minimum 20 mm gap maintained between insulation and sarking.
- (2) Eave ventilation opening in accordance with Table 10.8.3.

ROOF PLAN

1 : 100

Minimum pitch requirements for metal roofing profiles

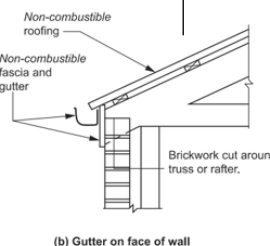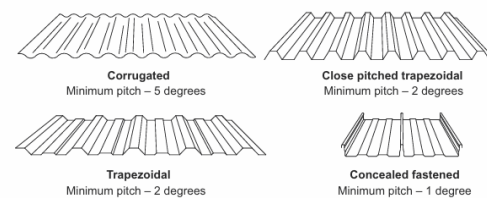


(b) Gutter on face of wall

Roof Schedule

Mark	Base Level	Area	Comments
R1	CEILING LEVEL	172 m ²	COLORBOND(GREY NON-REFLECTIVE)
R2	Level 1	39 m ²	COLORBOND(GREY NON-REFLECTIVE)
R3	Level 1	6 m ²	COLORBOND(GREY NON-REFLECTIVE)
Grand total: 3		217 m ²	

CC ISSUE


REV	DATE	DESCRIPTION	BY
5	31-07-2026	CC ISSUE	
4	29-06-2026	RFI 3 ISSUE	
3	16-06-2026	RFI 2 ISSUE	
2	26-05-2026	RFI ISSUE	
1	22-04-2026	DA ISSUE	

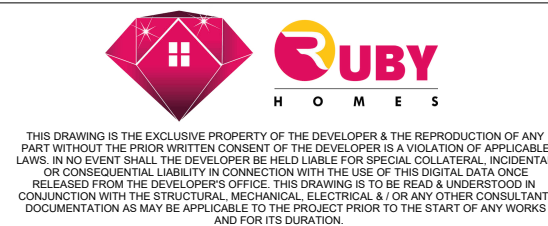



PROJECT:
Residential Dwelling

LOT 1008 IN DP 1306994
LOCATED AT No.16 Ridgeway Drive Orchard Hills NSW.

DRAWING TITLE:
ROOF PLAN

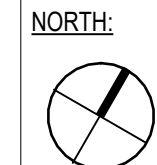

LOT NO: 1008	DATE: 11-08-2026	SCALE: 1 : 100	DRAWING No: CC.07	REV: 5
DRAWN BY: AS	CHECKED BY: RH			ISSUED BY:
DRAFTED BY: SL	CLIENT NAME: Saggita Reddy			

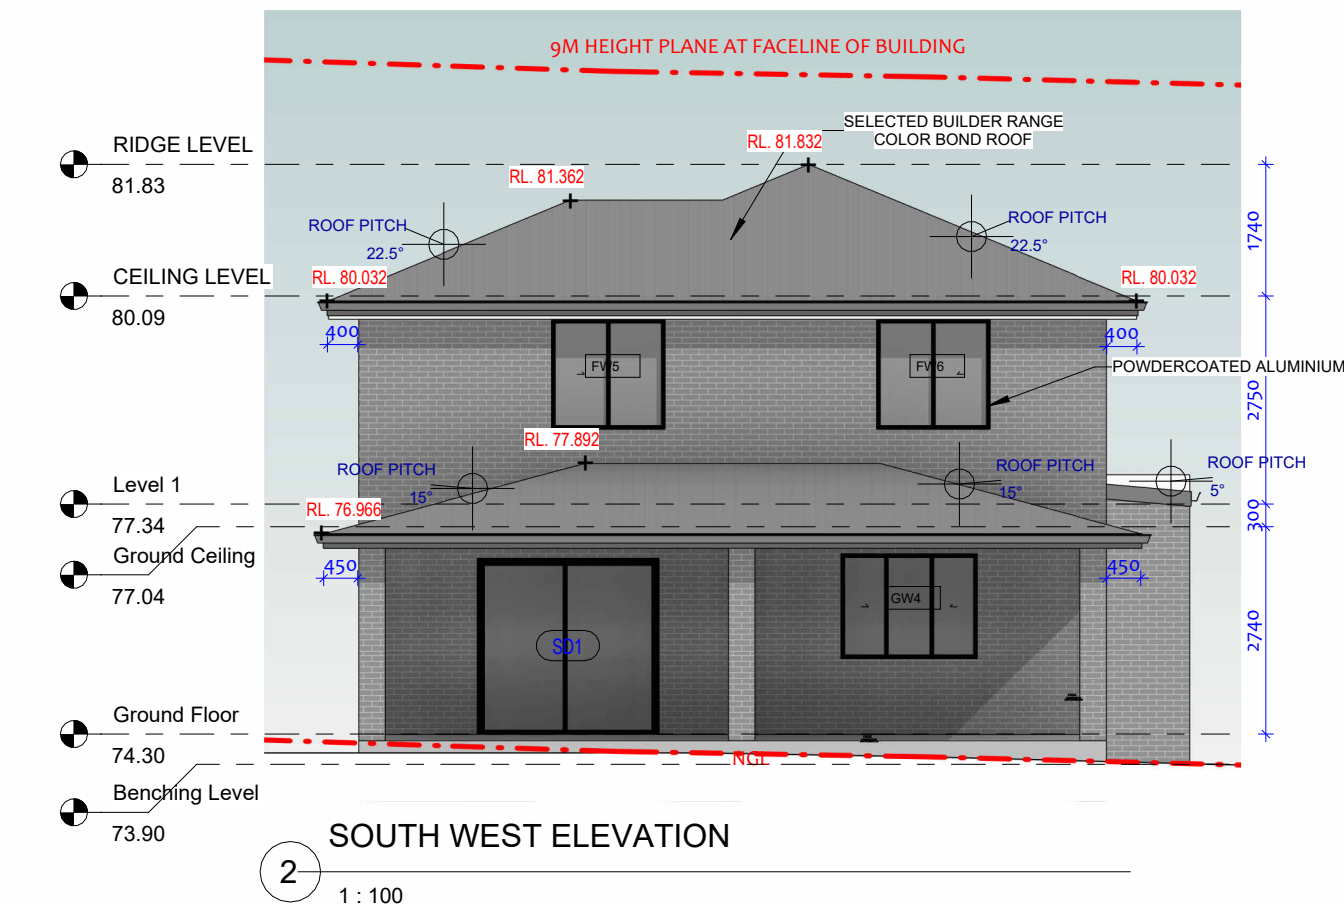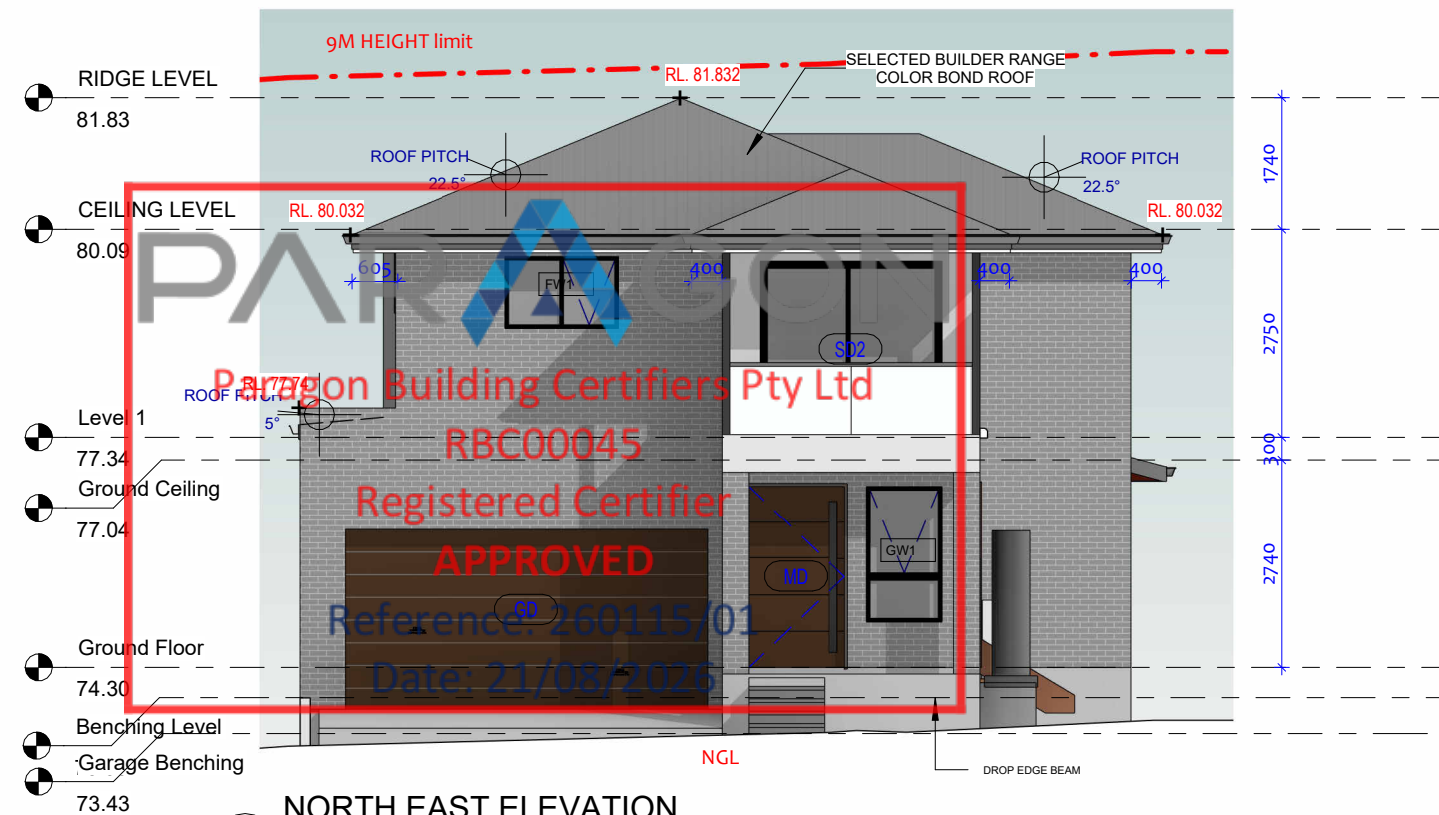

Window Schedule 1					
Mark	Height	Width	Sill Height	Head Height	Description

Ground Floor

GW1	1800	1000	600	2400	AWNING
GW2	800	800	1600	2400	SLIDING
GW3	1500	1800	900	2400	SLIDING
GW4	1400	1800	1000	2400	SLIDING
GW5	600	1800	900	1500	FIXED
GW6	600	900	950	1550	SLIDING
GW7	1400	1500	1000	2400	SLIDING

Ground Floor: 7

Level 1

FW1	950	1500	1450	2400	FIXED with AWNING
FW2	800	1500	1650	2450	SLIDING
FW3	2050	1200	400	2450	FIXED
FW4	600	800	1850	2450	SLIDING
FW5	1450	1500	1000	2450	SLIDING
FW6	1450	1500	1000	2450	SLIDING
FW7	800	1200	1650	2450	SLIDING
FW8	800	2200	1650	2450	SLIDING

Level 1: 8

Door Schedule 1				
Mark	Height	Width	Count	Description

Ground Floor

D1	2340	820	1	FLUSH DOOR
D2	2340	720	1	FLUSH DOOR
D3	2340	720	1	FLUSH DOOR
D4	2340	720	1	FLUSH DOOR
D5	2340	820	1	FLUSH DOOR
D6	2340	800	1	FLUSH DOOR
GD	2400	4800	1	GARAGE DOOR
MD	2400	1260	1	SOLID CORE DOOR
SD1	2300	2400	1	SLIDING DOOR

Ground Floor: 9

Level 1

D7	2340	820	1	FLUSH DOOR
D8	2340	820	1	FLUSH DOOR
D9	2340	720	1	FLUSH DOOR
D10	2340	720	1	FLUSH DOOR
D11	2340	820	1	FLUSH DOOR
D12	2340	820	1	FLUSH DOOR
D13	2340	720	1	FLUSH DOOR
SD2	2300	2400	1	SLIDING DOOR

Level 1: 8

REV	DATE	DESCRIPTION	BY
5	31-07-2026	CC ISSUE	
4	29-06-2026	RFI 3 ISSUE	
3	16-06-2026	RFI 2 ISSUE	
2	26-05-2026	RFI ISSUE	
1	22-04-2026	DA ISSUE	



THIS DRAWING IS THE EXCLUSIVE PROPERTY OF THE DEVELOPER & THE REPRODUCTION OF ANY PART WITHOUT THE PRIOR WRITTEN CONSENT OF THE DEVELOPER IS A VIOLATION OF APPLICABLE LAWS. IN NO EVENT SHALL THE DEVELOPER BE HELD LIABLE FOR SPECIAL COLLATERAL, INCIDENTAL OR CONSEQUENTIAL LIABILITY IN CONNECTION WITH THE USE OF THIS DIGITAL DATA ONCE RELEASED FROM THE DEVELOPER'S OFFICE. THIS DRAWING IS TO BE READ & UNDERSTOOD IN CONJUNCTION WITH THE STRUCTURAL, MECHANICAL, ELECTRICAL & / OR ANY OTHER CONSULTANT'S DOCUMENTATION AS MAY BE APPLICABLE TO THE PROJECT PRIOR TO THE START OF ANY WORKS AND FOR ITS DURATION.

PROJECT:
Residential Dwelling

**LOT 1008 IN DP 1306994
LOCATED AT No.16 Ridgeway
Drive Orchard Hills NSW.**

DRAWING TITLE:
ELEVATION 01

NORTH:

LOT NO:
1008

DRAWN BY:
AS

DRAFTED BY:
SL

DATE:
11-08-2026

CHECKED BY:
RH

CLIENT NAME:
Saggita Reddy


SCALE:
1 : 100

DRAWING No:
CC.08

REV:
5

ISSUED BY:


CC ISSUE

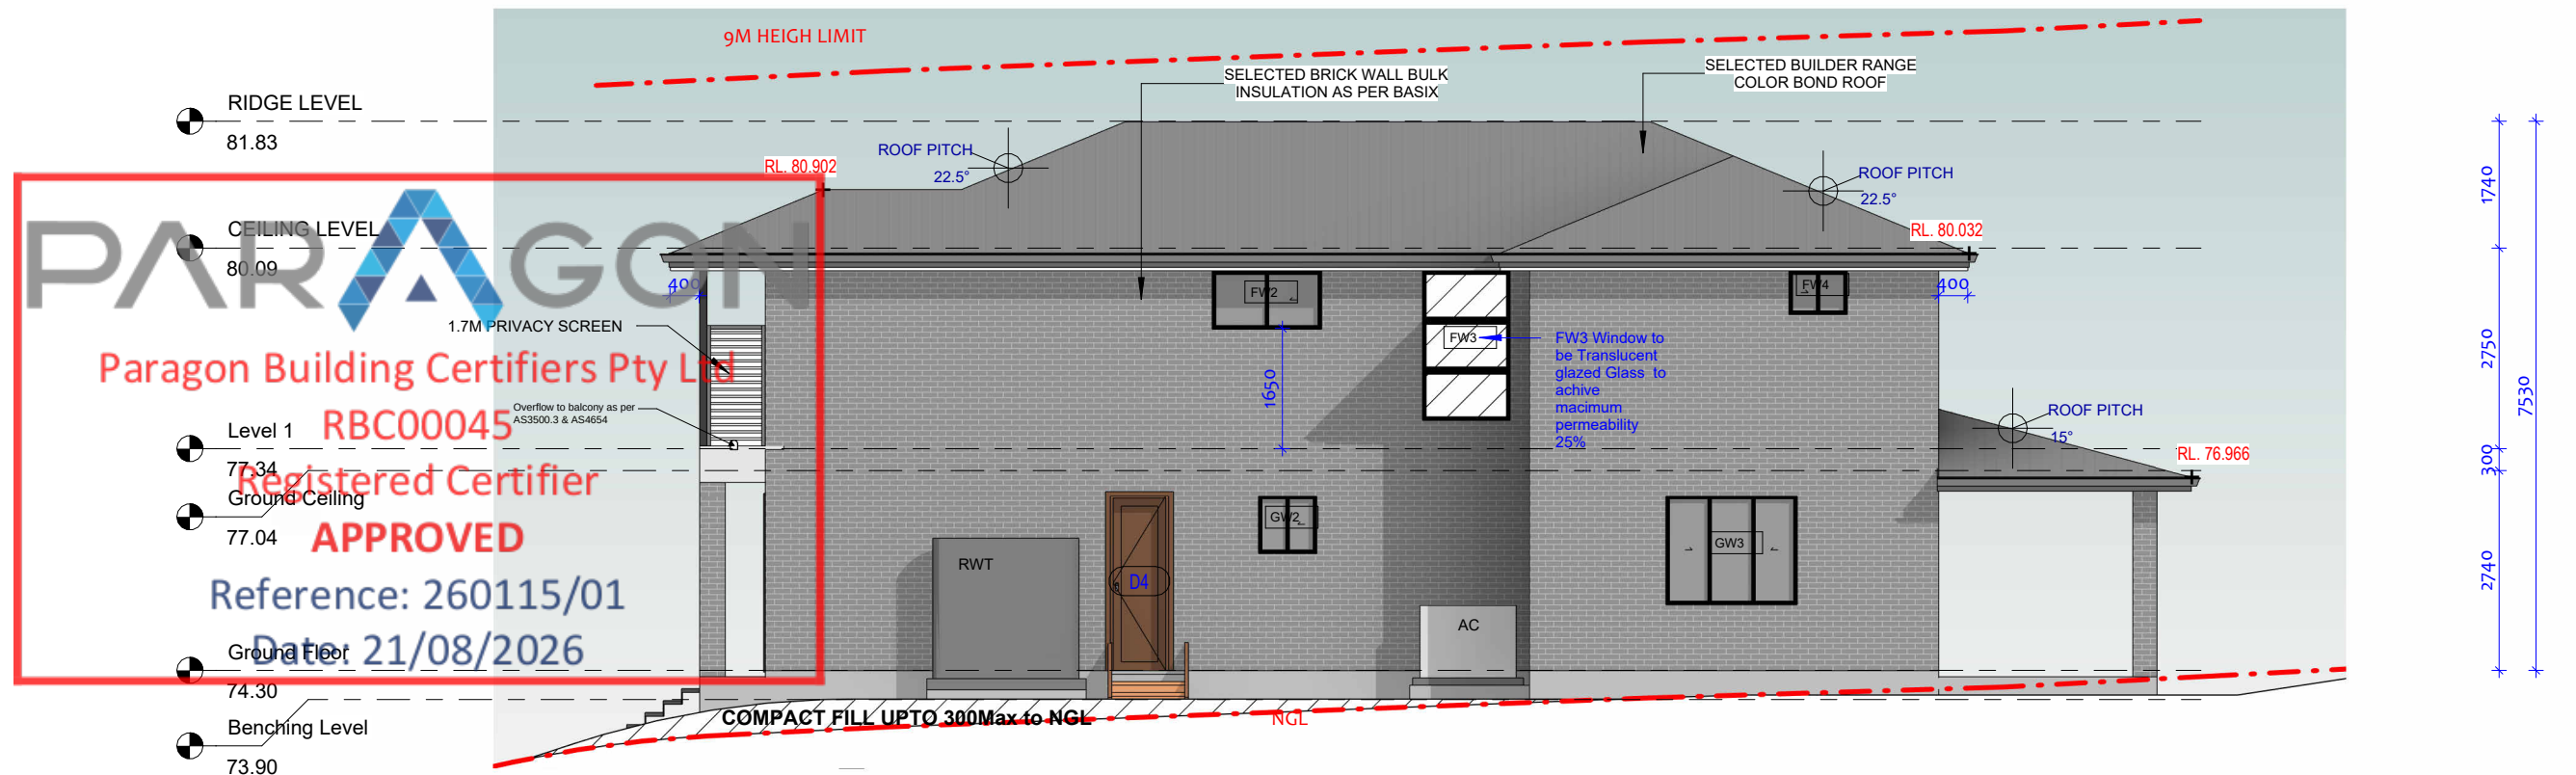

NORTH WEST ELEVATION

1

1 : 100

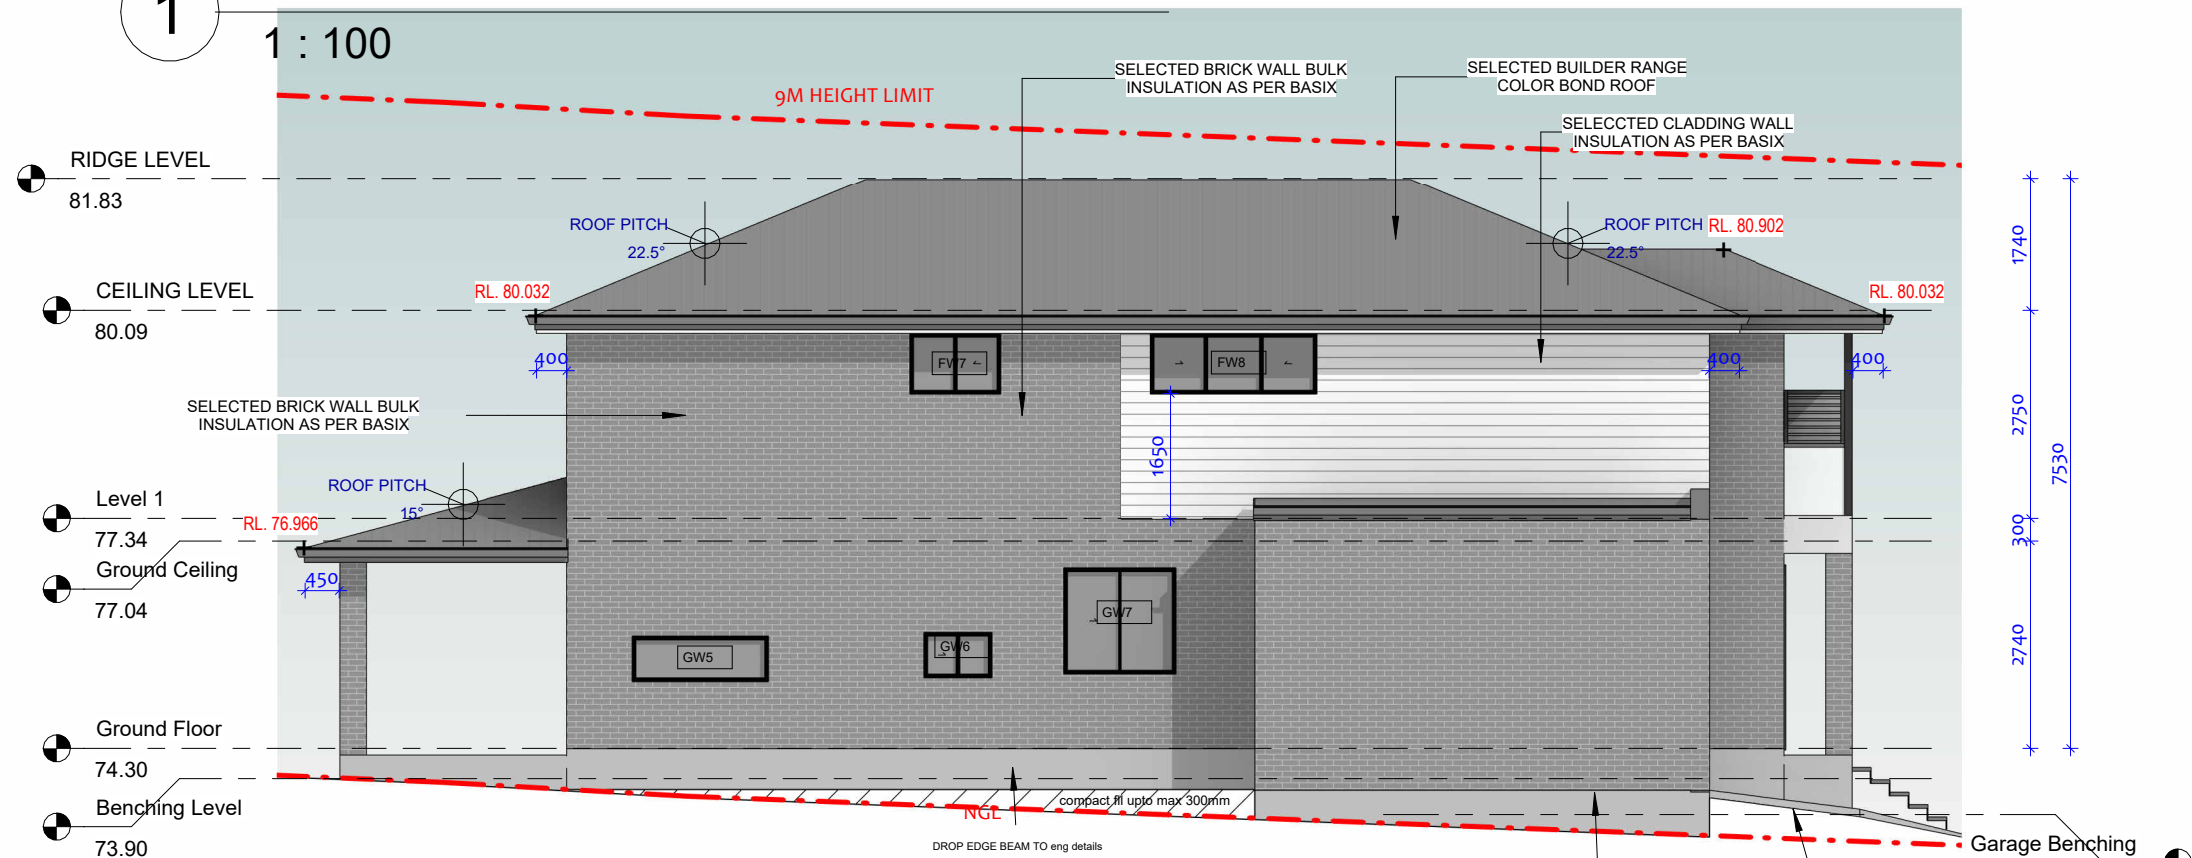

SOUTH EAST ELEVATION

2

1 : 100

REV	DATE	DESCRIPTION	BY
5	31-07-2026	CC ISSUE	
4	29-06-2026	RFI 3 ISSUE	
3	16-06-2026	RFI 2 ISSUE	
2	26-05-2026	RFI ISSUE	
1	22-04-2026	DA ISSUE	

RUBY HOMES

THIS DRAWING IS THE EXCLUSIVE PROPERTY OF THE DEVELOPER & THE REPRODUCTION OF ANY PART WITHOUT THE PRIOR WRITTEN CONSENT OF THE DEVELOPER IS A VIOLATION OF APPLICABLE LAWS. IN NO EVENT SHALL THE DEVELOPER BE HELD LIABLE FOR SPECIAL COLLATERAL, INCIDENTAL OR CONSEQUENTIAL LIABILITY IN CONNECTION WITH THE USE OF THIS DIGITAL DATA ONCE RELEASED FROM THE DEVELOPER'S OFFICE. THIS DRAWING IS TO BE READ & UNDERSTOOD IN CONJUNCTION WITH THE STRUCTURAL, MECHANICAL, ELECTRICAL & / OR ANY OTHER CONSULTANT'S DOCUMENTATION AS MAY BE APPLICABLE TO THE PROJECT PRIOR TO THE START OF ANY WORKS AND FOR ITS DURATION.

PROJECT:
Residential Dwelling


**LOT 1008 IN DP 1306994
LOCATED AT No.16 Ridgeway
Drive Orchard Hills NSW.**

DRAWING TITLE:
ELEVATION 02

NORTH:


LOT NO: 1008	DATE: 11-08-2026	SCALE: 1 : 100	DRAWING No: CC.09	REV: 5
DRAWN BY: AS	CHECKED BY: RH			ISSUED BY:
DRAFTED BY: SL	CLIENT NAME: Saggita Reddy			

CC ISSUE

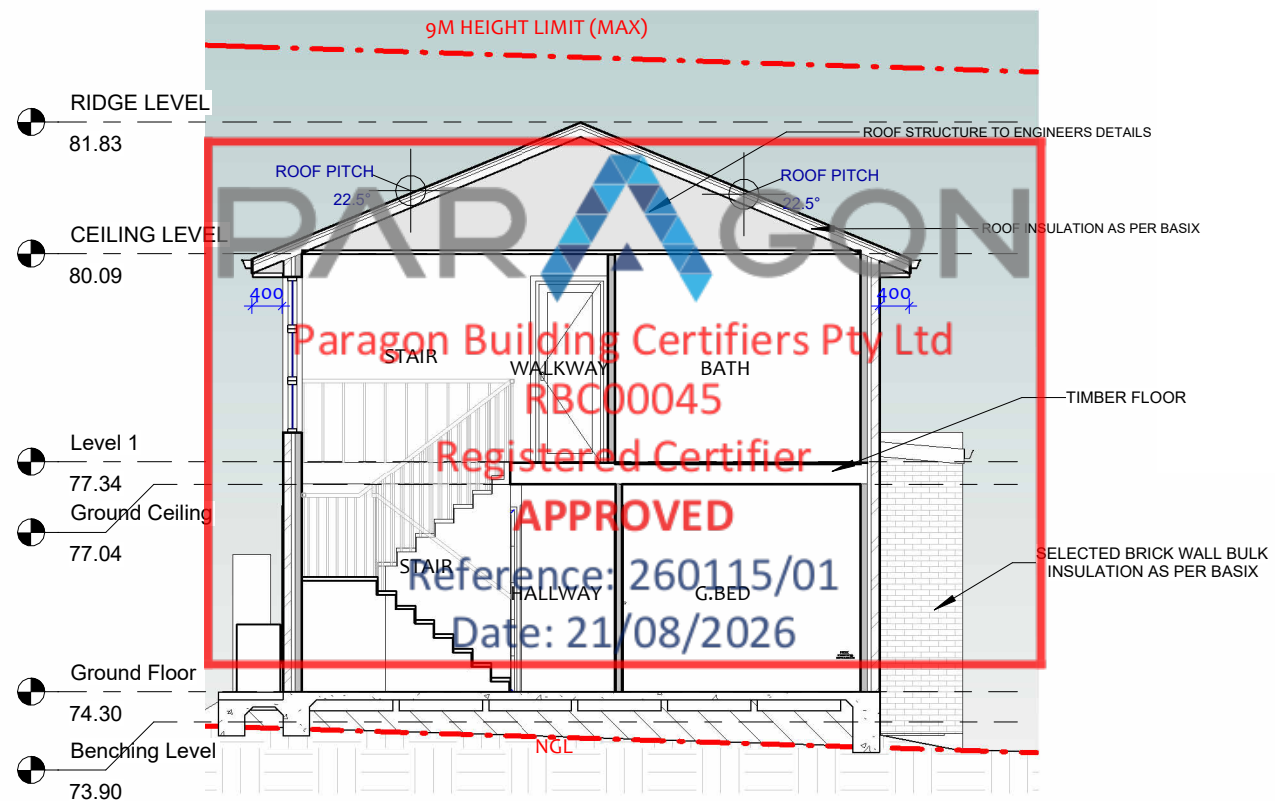

CROSS SECTION

1
1 : 100

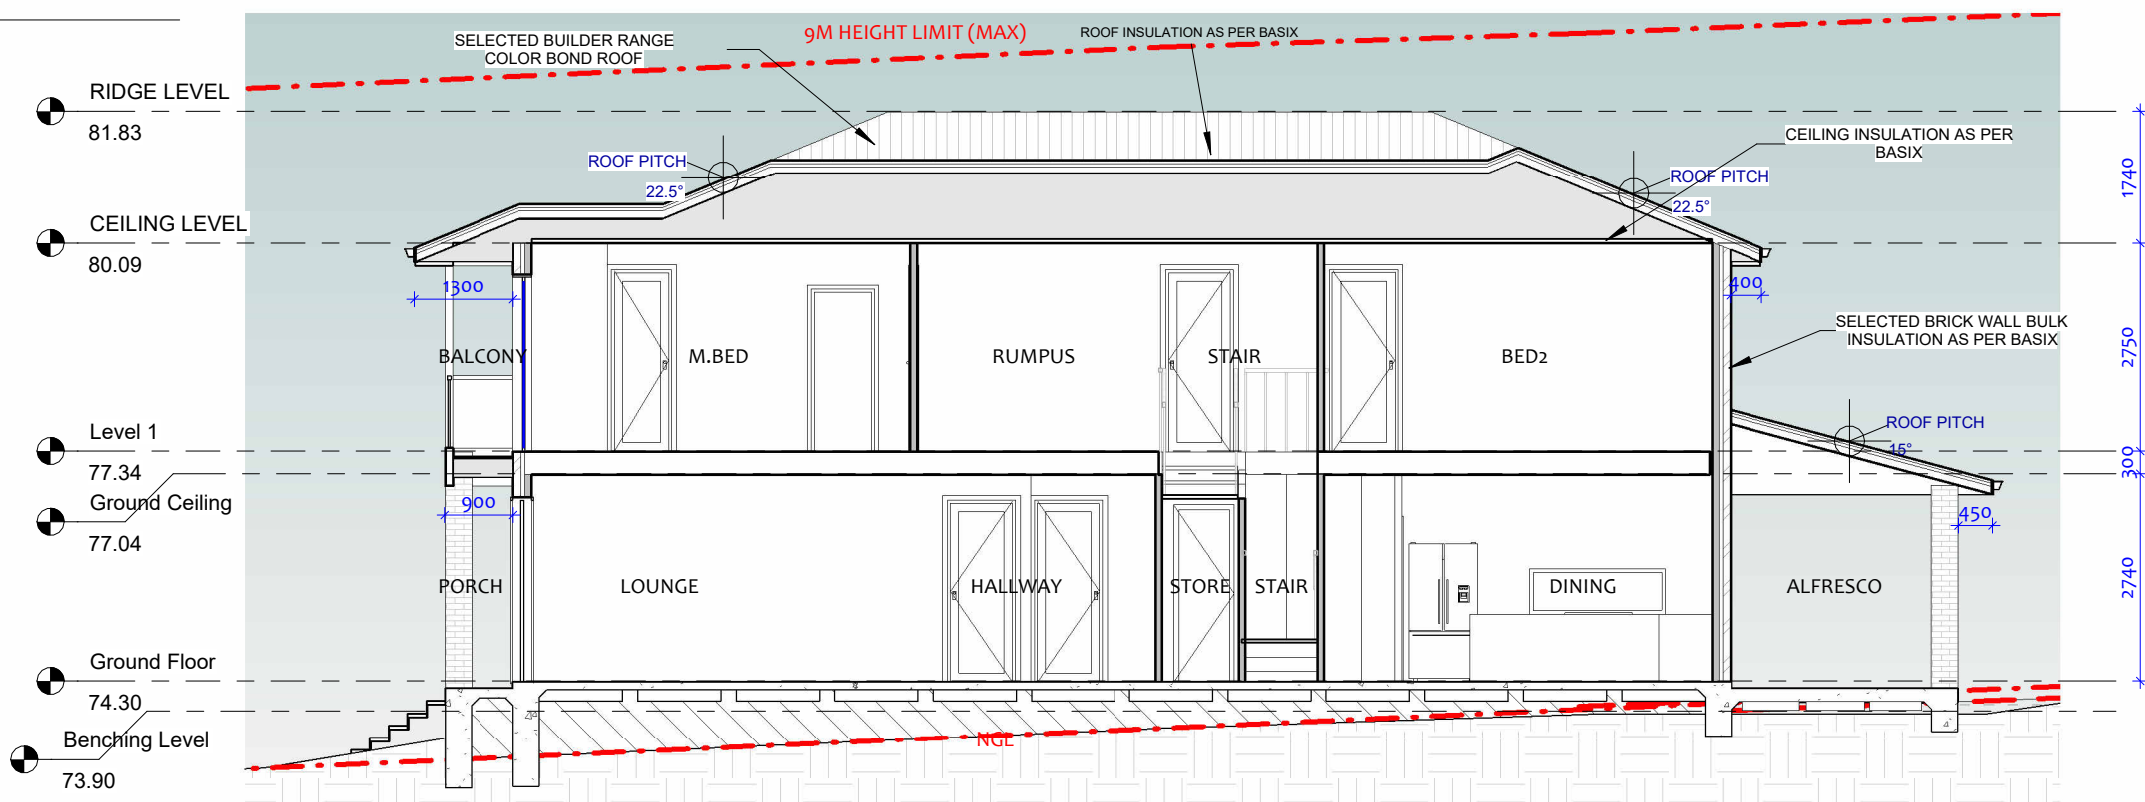

LONGITUDINAL SECTION

2
1 : 100

REV	DATE	DESCRIPTION	BY
5	31-07-2026	CC ISSUE	
4	29-06-2026	RFI 3 ISSUE	
3	16-06-2026	RFI 2 ISSUE	
2	26-05-2026	RFI ISSUE	
1	22-04-2026	DA ISSUE	



 THIS DRAWING IS THE EXCLUSIVE PROPERTY OF THE DEVELOPER & THE REPRODUCTION OF ANY PART WITHOUT THE PRIOR WRITTEN CONSENT OF THE DEVELOPER IS A VIOLATION OF APPLICABLE LAWS. IN NO EVENT SHALL THE DEVELOPER BE HELD LIABLE FOR SPECIAL COLLATERAL, INCIDENTAL OR CONSEQUENTIAL LIABILITY IN CONNECTION WITH THE USE OF THIS DIGITAL DATA ONCE RELEASED FROM THE DEVELOPER'S OFFICE. THIS DRAWING IS TO BE READ & UNDERSTOOD IN CONJUNCTION WITH THE STRUCTURAL, MECHANICAL, ELECTRICAL & / OR ANY OTHER CONSULTANT'S DOCUMENTATION AS MAY BE APPLICABLE TO THE PROJECT PRIOR TO THE START OF ANY WORKS AND FOR ITS DURATION.

PROJECT:
 Residential Dwelling
 LOT 1008 IN DP 1306994
 LOCATED AT No.16 Ridgeway
 Drive Orchard Hills NSW.

DRAWING TITLE:
 SECTIONS

NORTH:


LOT NO:
 1008
 DRAWN BY:
 AS
 DRAFTED BY:
 SL

DATE:
 11-08-2026
 CHECKED BY:
 RH
 CLIENT NAME:
 Saggita Reddy

SCALE:
 1 : 100

DRAWING No:
 CC.10
 REV:
 5
 ISSUED BY:

CC ISSUE

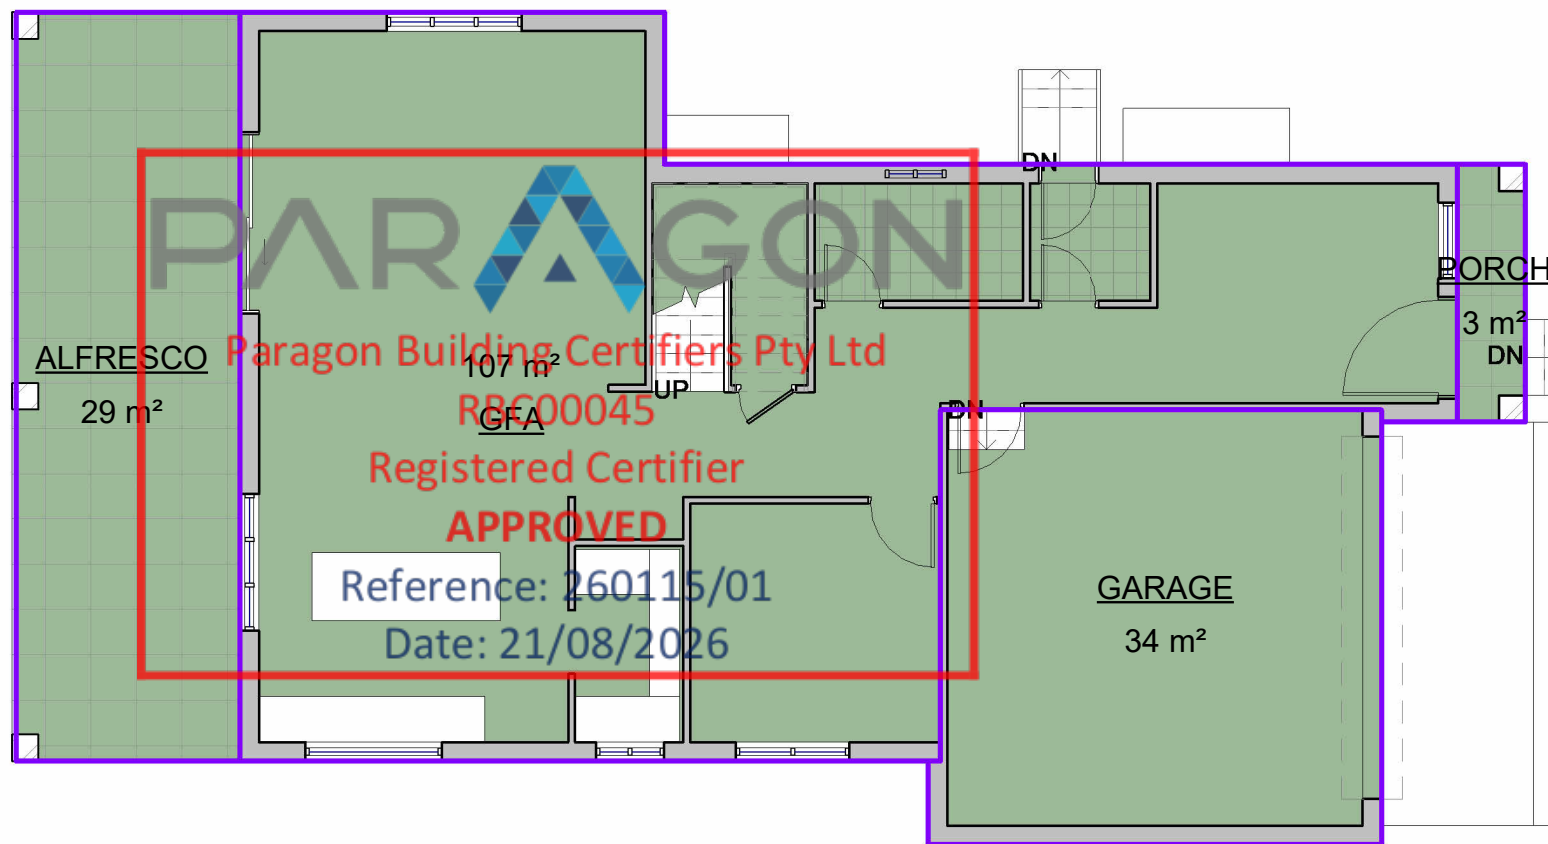

Area Schedule (Gross Building)	
Name	Area

Ground Floor

GFA	107 m²
GARAGE	34 m²
PORCH	3 m²
ALFRESCO	29 m²

Ground Floor: 4 173 m²

Level 1


FFA	134 m²
BALCONY	3 m²

Level 1: 2 137 m²

Grand total: 6 310 m²

Ground Floor

1
1 : 100

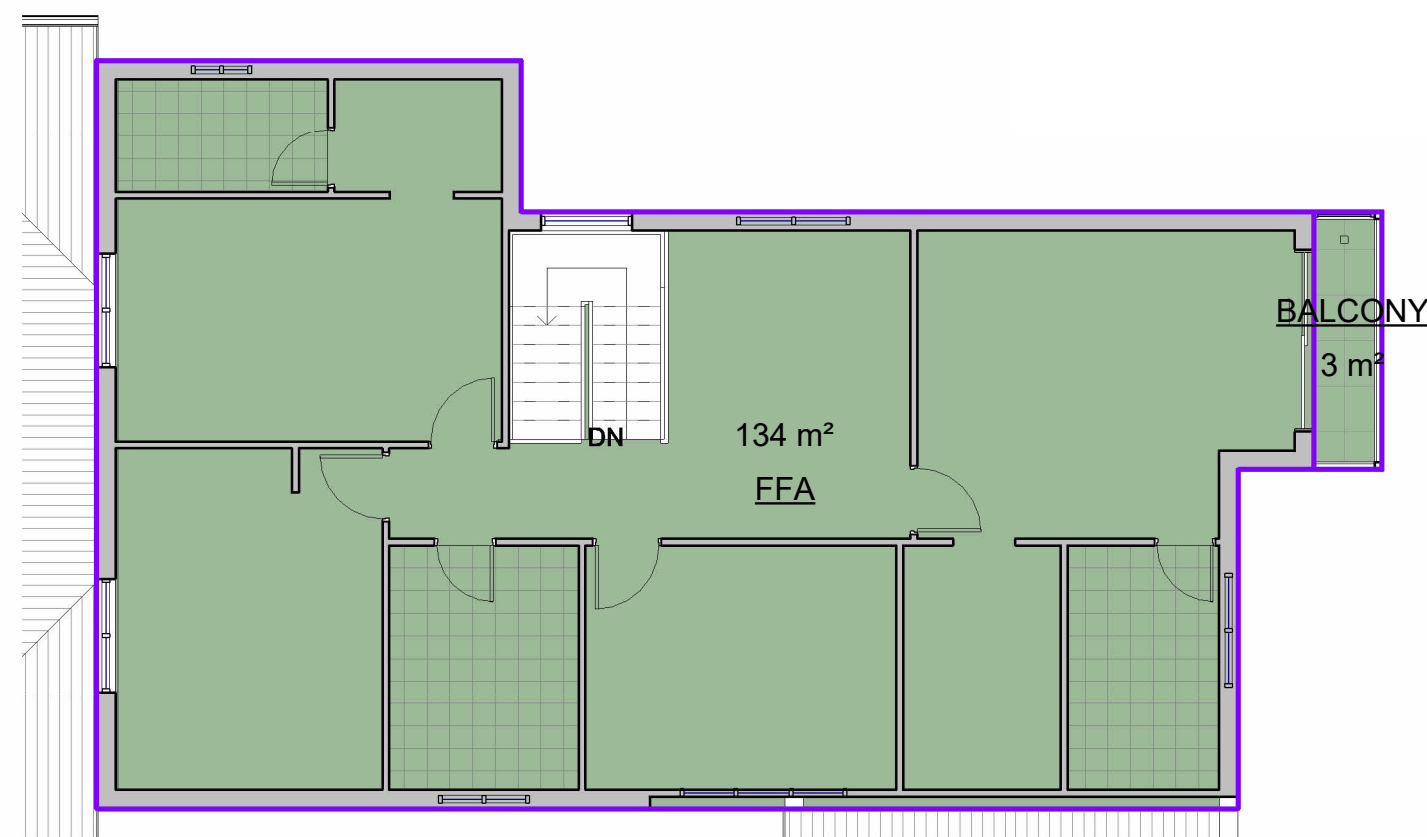

Level 1

2
1 : 100

REV	DATE	DESCRIPTION	BY
5	31-07-2026	CC ISSUE	
4	29-06-2026	RFI 3 ISSUE	
3	16-06-2026	RFI 2 ISSUE	
2	26-05-2026	RFI ISSUE	
1	22-04-2026	DA ISSUE	




THIS DRAWING IS THE EXCLUSIVE PROPERTY OF THE DEVELOPER & THE REPRODUCTION OF ANY PART WITHOUT THE PRIOR WRITTEN CONSENT OF THE DEVELOPER IS A VIOLATION OF APPLICABLE LAWS. IN NO EVENT SHALL THE DEVELOPER BE HELD LIABLE FOR SPECIAL COLLATERAL, INCIDENTAL OR CONSEQUENTIAL LIABILITY IN CONNECTION WITH THE USE OF THIS DIGITAL DATA ONCE RELEASED FROM THE DEVELOPER'S OFFICE. THIS DRAWING IS TO BE READ & UNDERSTOOD IN CONJUNCTION WITH THE STRUCTURAL, MECHANICAL, ELECTRICAL & / OR ANY OTHER CONSULTANT'S DOCUMENTATION AS MAY BE APPLICABLE TO THE PROJECT PRIOR TO THE START OF ANY WORKS AND FOR ITS DURATION.

PROJECT:
 Residential Dwelling
LOT 1008 IN DP 1306994
LOCATED AT No.16 Ridgeway Drive Orchard Hills NSW.

DRAWING TITLE:
FLOOR AREA PLAN




LOT NO:
 1008
DRAWN BY:
 AS
DRAFTED BY:
 SL

DATE:
 11-08-2026
CHECKED BY:
 RH
CLIENT NAME:
 Saggita Reddy


SCALE:
 1 : 100

DRAWING No:
 CC.11
REV:
 5
ISSUED BY:

CC ISSUE

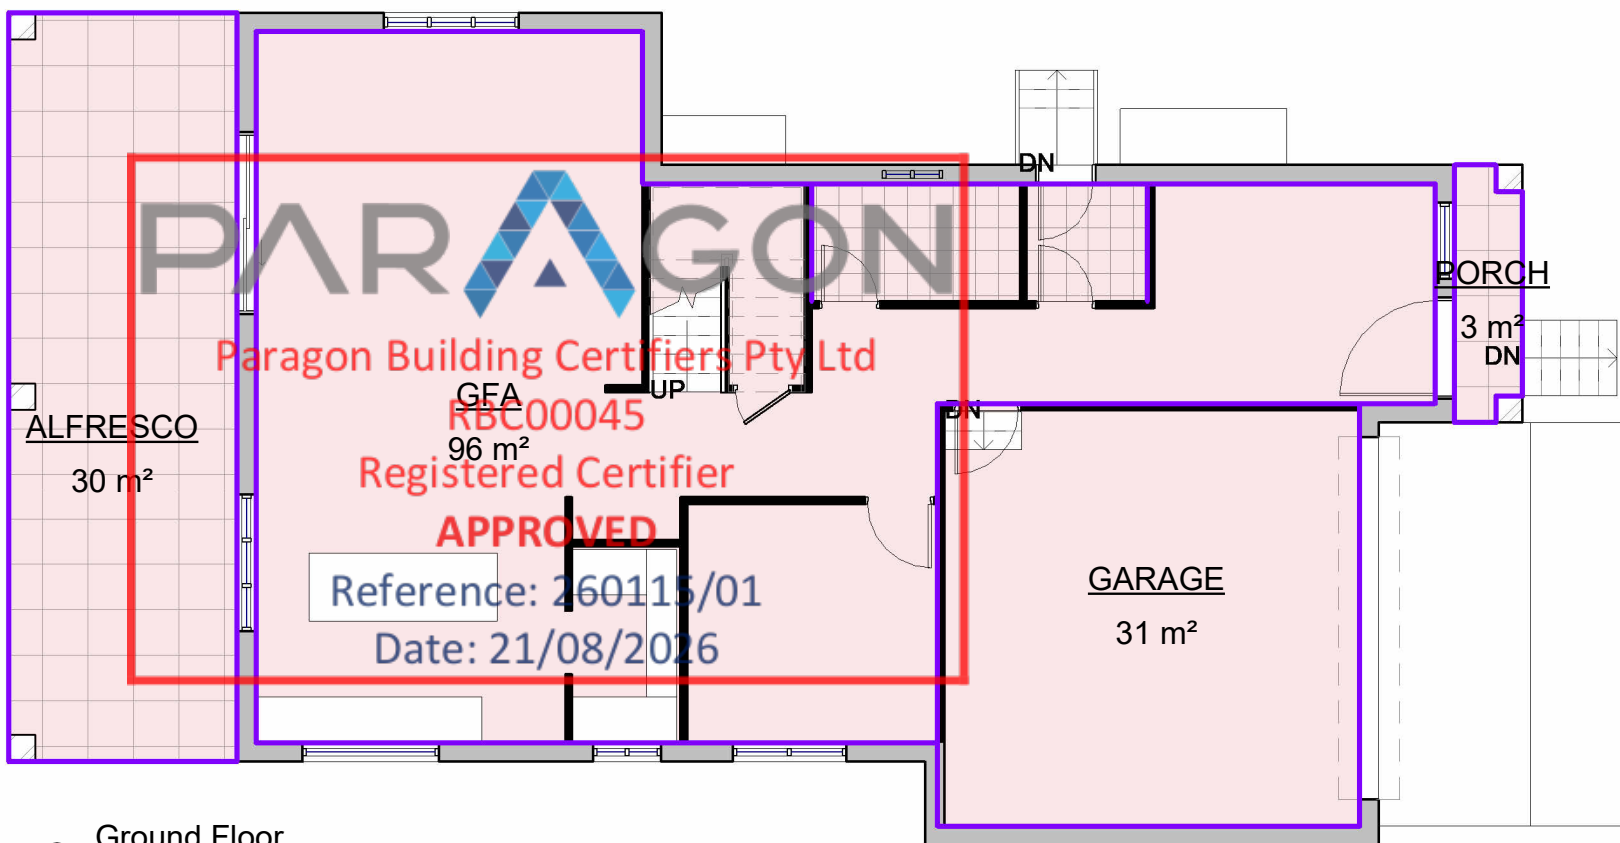

1 Ground Floor
1 : 100

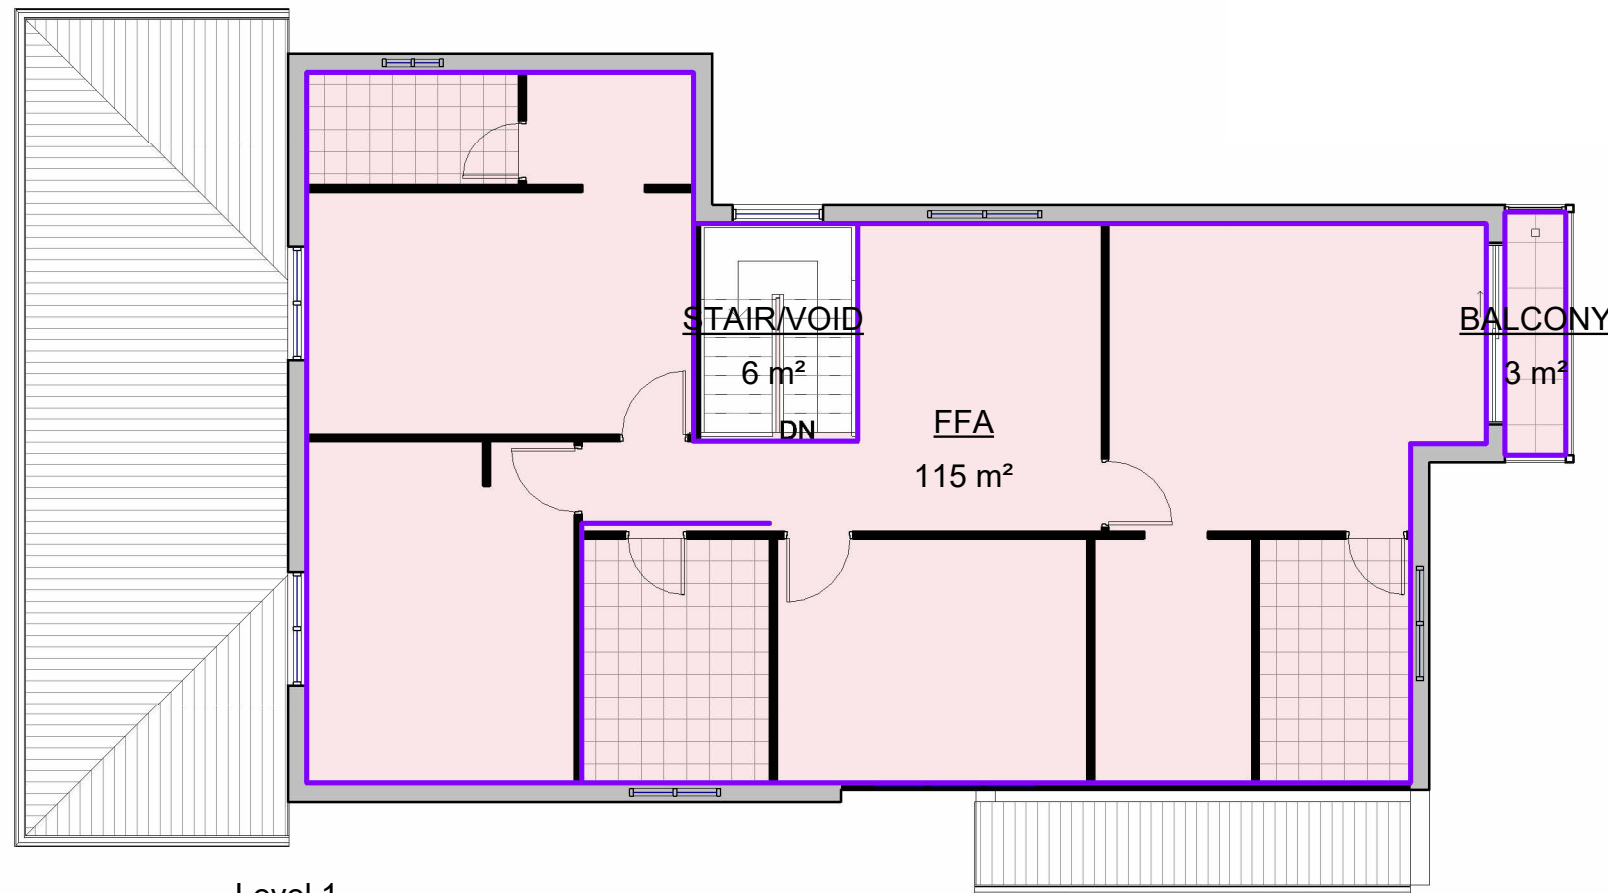

2 Level 1
1 : 100

Area Schedule (Rentable)	
Name	Area

Ground Floor

GFA	96 m²
GARAGE	31 m²
ALFRESCO	30 m²
PORCH	3 m²

Ground Floor: 4 160 m²

Level 1

BALCONY	3 m²
FFA	115 m²
STAIR/VOID	6 m²

Level 1: 3 124 m²

Grand total: 7 283 m²

REV	DATE	DESCRIPTION	BY
5	31-07-2026	CC ISSUE	
4	29-06-2026	RFI 3 ISSUE	
3	16-06-2026	RFI 2 ISSUE	
2	26-05-2026	RFI ISSUE	
1	22-04-2026	DA ISSUE	


THIS DRAWING IS THE EXCLUSIVE PROPERTY OF THE DEVELOPER & THE REPRODUCTION OF ANY PART WITHOUT THE PRIOR WRITTEN CONSENT OF THE DEVELOPER IS A VIOLATION OF APPLICABLE LAWS. IN NO EVENT SHALL THE DEVELOPER BE HELD LIABLE FOR SPECIAL COLLATERAL, INCIDENTAL OR CONSEQUENTIAL LIABILITY IN CONNECTION WITH THE USE OF THIS DIGITAL DATA ONCE RELEASED FROM THE DEVELOPER'S OFFICE. THIS DRAWING IS TO BE READ & UNDERSTOOD IN CONJUNCTION WITH THE STRUCTURAL, MECHANICAL, ELECTRICAL & / OR ANY OTHER CONSULTANT'S DOCUMENTATION AS MAY BE APPLICABLE TO THE PROJECT PRIOR TO THE START OF ANY WORKS AND FOR ITS DURATION.

RUBY HOMES

PROJECT:
Residential Dwelling


LOT 1008 IN DP 1306994
LOCATED AT No.16 Ridgeway Drive Orchard Hills NSW.

DRAWING TITLE:
RENTABLE AREA PLAN

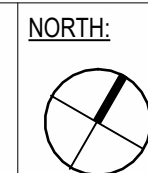


LOT NO: 1008	DATE: 11-08-2026	SCALE: 1 : 100	DRAWING No: CC.12	REV: 5
DRAWN BY: AS	CHECKED BY: RH			ISSUED BY:
DRAFTED BY: SL	CLIENT NAME: Saggita Reddy			

CC ISSUE

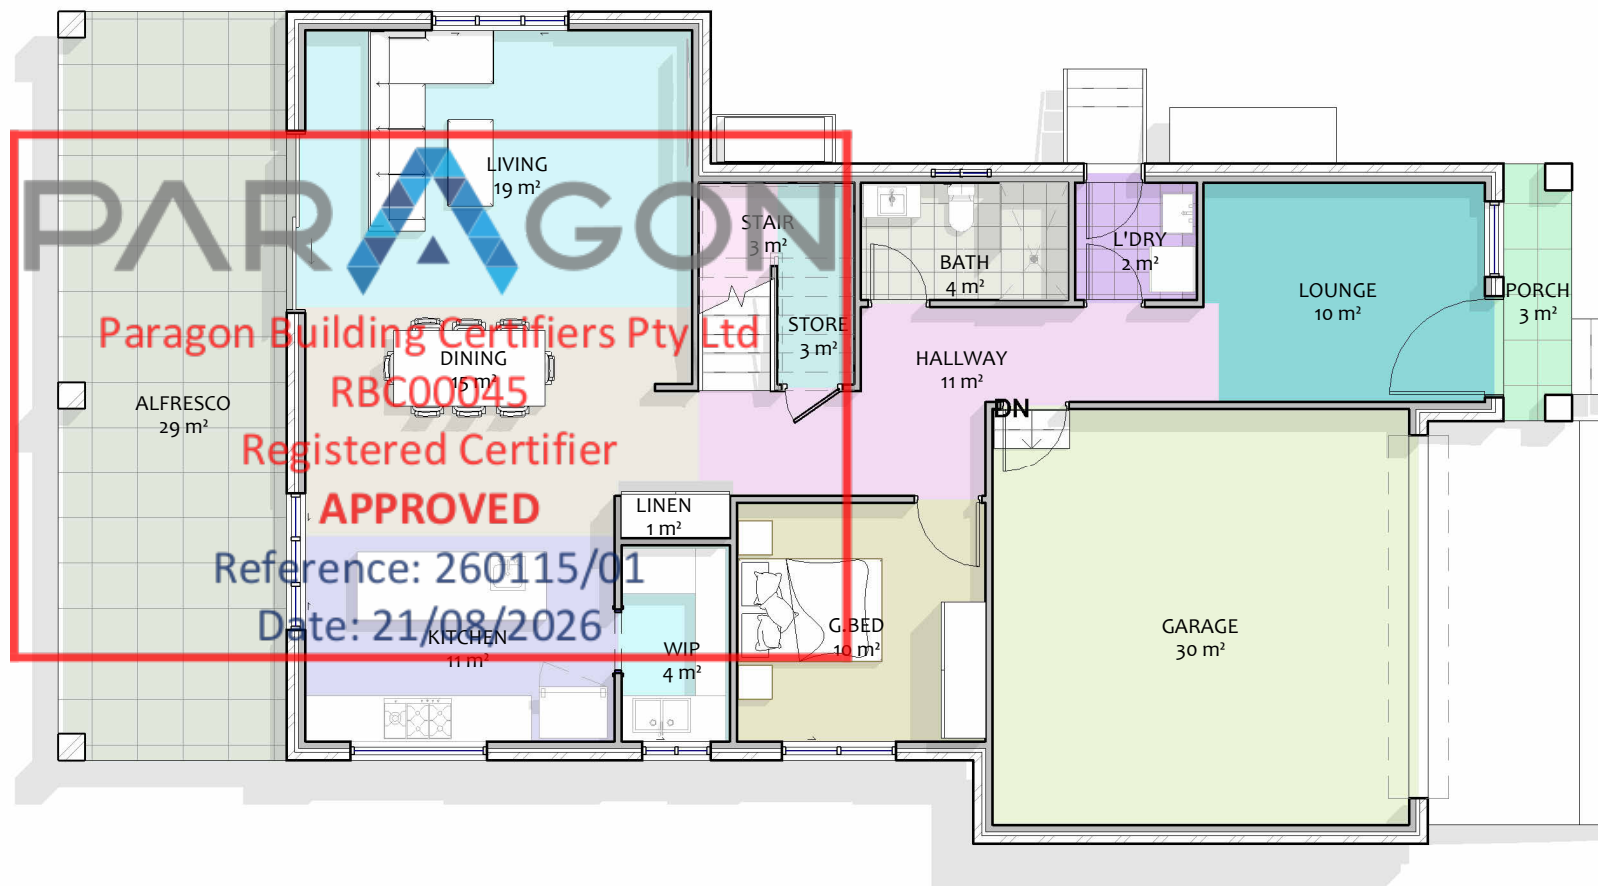

Ground Floor Room Area Plan

1
1 : 100

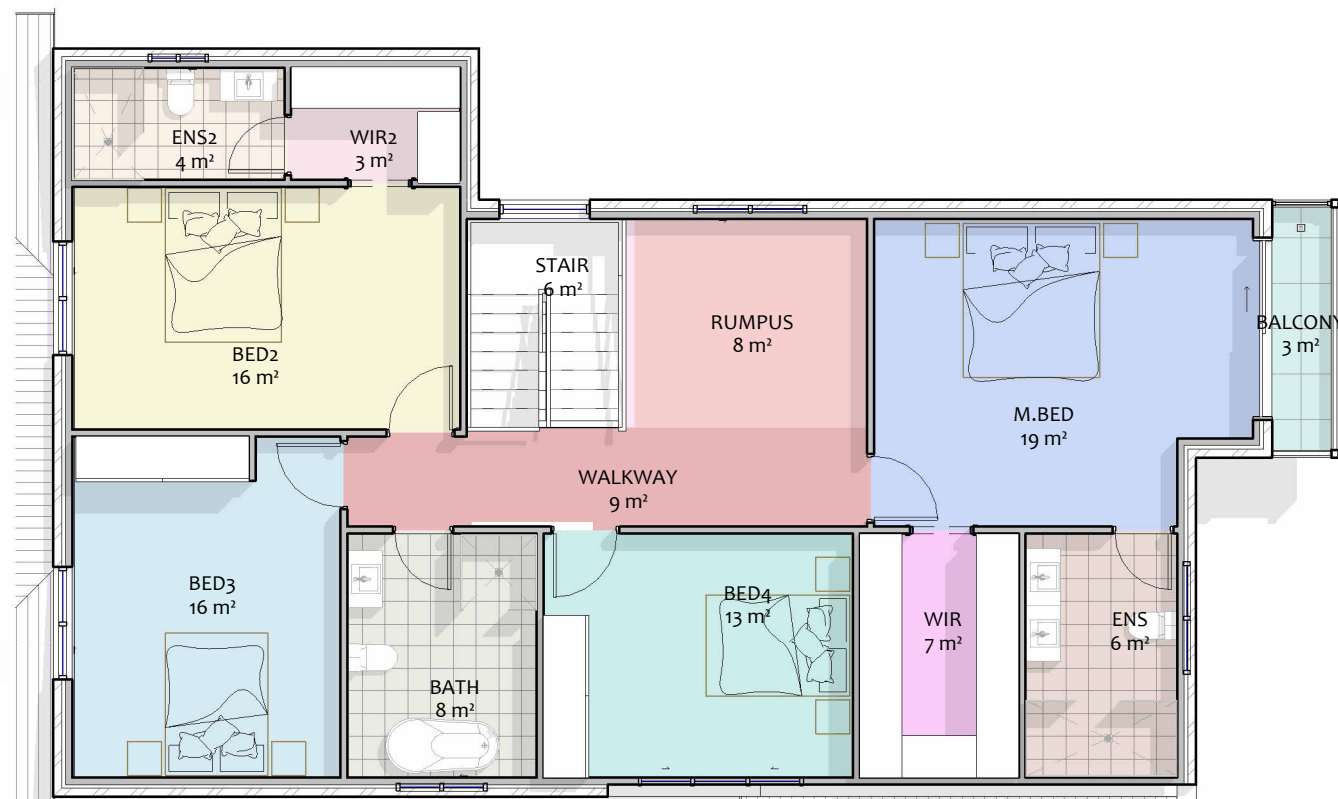

Level 1 Room Area Plan

2
1 : 100

Room Schedule

Name	Area
------	------

Ground Floor

ALFRESCO	29 m ²
BATH	4 m ²
DINING	15 m ²
G.BED	10 m ²
GARAGE	30 m ²
HALLWAY	11 m ²
KITCHEN	11 m ²
L'DRY	2 m ²
LINEN	1 m ²
LIVING	19 m ²
LOUNGE	10 m ²
PORCH	3 m ²
STAIR	3 m ²
STORE	3 m ²
WIP	4 m ²

Ground Floor: 15 156 m²

Level 1

BALCONY	3 m ²
BATH	8 m ²
BED2	16 m ²
BED3	16 m ²
BED4	13 m ²
ENS	6 m ²
ENS2	4 m ²
M.BED	19 m ²
RUMPUS	8 m ²
STAIR	6 m ²
WALKWAY	9 m ²
WIR	7 m ²
WIR2	3 m ²

Level 1: 13 120 m²

Grand total 275 m²

REV	DATE	DESCRIPTION	BY
5	31-07-2026	CC ISSUE	
4	29-06-2026	RFI 3 ISSUE	
3	16-06-2026	RFI 2 ISSUE	
2	26-05-2026	RFI ISSUE	
1	22-04-2026	DA ISSUE	

PARAGON
Paragon Building Certifiers Pty Ltd
RBC00045
Registered Certifier
APPROVED
Reference: 260115/01
Date: 21/08/2026

RUBY HOMES

THIS DRAWING IS THE EXCLUSIVE PROPERTY OF THE DEVELOPER & THE REPRODUCTION OF ANY PART WITHOUT THE PRIOR WRITTEN CONSENT OF THE DEVELOPER IS A VIOLATION OF APPLICABLE LAWS. IN NO EVENT SHALL THE DEVELOPER BE HELD LIABLE FOR SPECIAL COLLATERAL, INCIDENTAL OR CONSEQUENTIAL LIABILITY IN CONNECTION WITH THE USE OF THIS DIGITAL DATA ONCE RELEASED FROM THE DEVELOPER'S OFFICE. THIS DRAWING IS TO BE READ & UNDERSTOOD IN CONJUNCTION WITH THE STRUCTURAL, MECHANICAL, ELECTRICAL & / OR ANY OTHER CONSULTANT'S DOCUMENTATION AS MAY BE APPLICABLE TO THE PROJECT PRIOR TO THE START OF ANY WORKS AND FOR ITS DURATION.

PROJECT:
Residential Dwelling

**LOT 1008 IN DP 1306994
LOCATED AT No.16 Ridgeway
Drive Orchard Hills NSW.**

DRAWING TITLE:
ROOM AREA PLAN



LOT NO:	1008	DATE:	11-08-2026	SCALE:	1 : 100	DRAWING No:	CC.13	REV:	5
DRAWN BY:	AS	CHECKED BY:	RH					ISSUED BY:	
DRAFTED BY:	SL	CLIENT NAME:	Saggita Reddy						

PARAGON

Paragon Building Certifiers Pty Ltd

RBC00045

Registered Certifier

APPROVED

Reference: 260115/01

Date: 21/08/2026



	1. RF	2. BR1	3. CD1	4. CR1	5. AL	6. ED	7. GD	8. FAS	9. GUT
	ROOF	MAIN WALLS	CLADDING	ACCENT 1/RENDER	WINDOWS/ BALUSTRADE	MAIN DOOR	GARAGE DOOR	FASCIA	GUTTER
MATERIAL	COLORBOND	BRICK	BLUEBOARD	BRICK	COLORBOND	TIMBER	COLORBOND	COLORBOND	COLORBOND
COLOUR									
	shale grey	Wilderness Design Silver Birch	Lexicon Half SW1G2	Lexicon Half SW1G2	Woodland Grey	Woodland Grey	Woodland Grey	Woodland Grey	WALLABY

NOTE : ALL COLOURS SPECIFIED ARE INDICATIVE ONLY AND ARE SUBJECT TO VARIATION AND TO AVAILABILITY
ANY DISCREPANCY PLEASE FOLLOW AS PER RENDERED IMAGE

REV	DATE	DESCRIPTION	BY
5	31-07-2026	CC ISSUE	
4	29-06-2026	RFI 3 ISSUE	
3	16-06-2026	RFI 2 ISSUE	
2	26-05-2026	RFI ISSUE	
1	22-04-2026	DA ISSUE	



THIS DRAWING IS THE EXCLUSIVE PROPERTY OF THE DEVELOPER & THE REPRODUCTION OF ANY PART WITHOUT THE PRIOR WRITTEN CONSENT OF THE DEVELOPER IS A VIOLATION OF APPLICABLE LAWS. IN NO EVENT SHALL THE DEVELOPER BE HELD LIABLE FOR SPECIAL COLLATERAL, INCIDENTAL OR CONSEQUENTIAL LIABILITY IN CONNECTION WITH THE USE OF THIS DIGITAL DATA ONCE RELEASED FROM THE DEVELOPER'S OFFICE. THIS DRAWING IS TO BE READ & UNDERSTOOD IN CONJUNCTION WITH THE STRUCTURAL, MECHANICAL, ELECTRICAL & / OR ANY OTHER CONSULTANT'S DOCUMENTATION AS MAY BE APPLICABLE TO THE PROJECT PRIOR TO THE START OF ANY WORKS AND FOR ITS DURATION.

PROJECT:
Residential Dwelling


**LOT 1008 IN DP 1306994
LOCATED AT No.16 Ridgeway
Drive Orchard Hills NSW.**

DRAWING TITLE:
COLOR SCHEDULE




NORTH:

LOT NO:	DATE:	SCALE:	DRAWING No:	REV:
1008	11-08-2026	1 : 100	CC.14	5
DRAWN BY:	CHECKED BY:			ISSUED BY:
AS	RH			
DRAFTED BY:	CLIENT NAME:			
SL	Saggita Reddy			

CC ISSUE

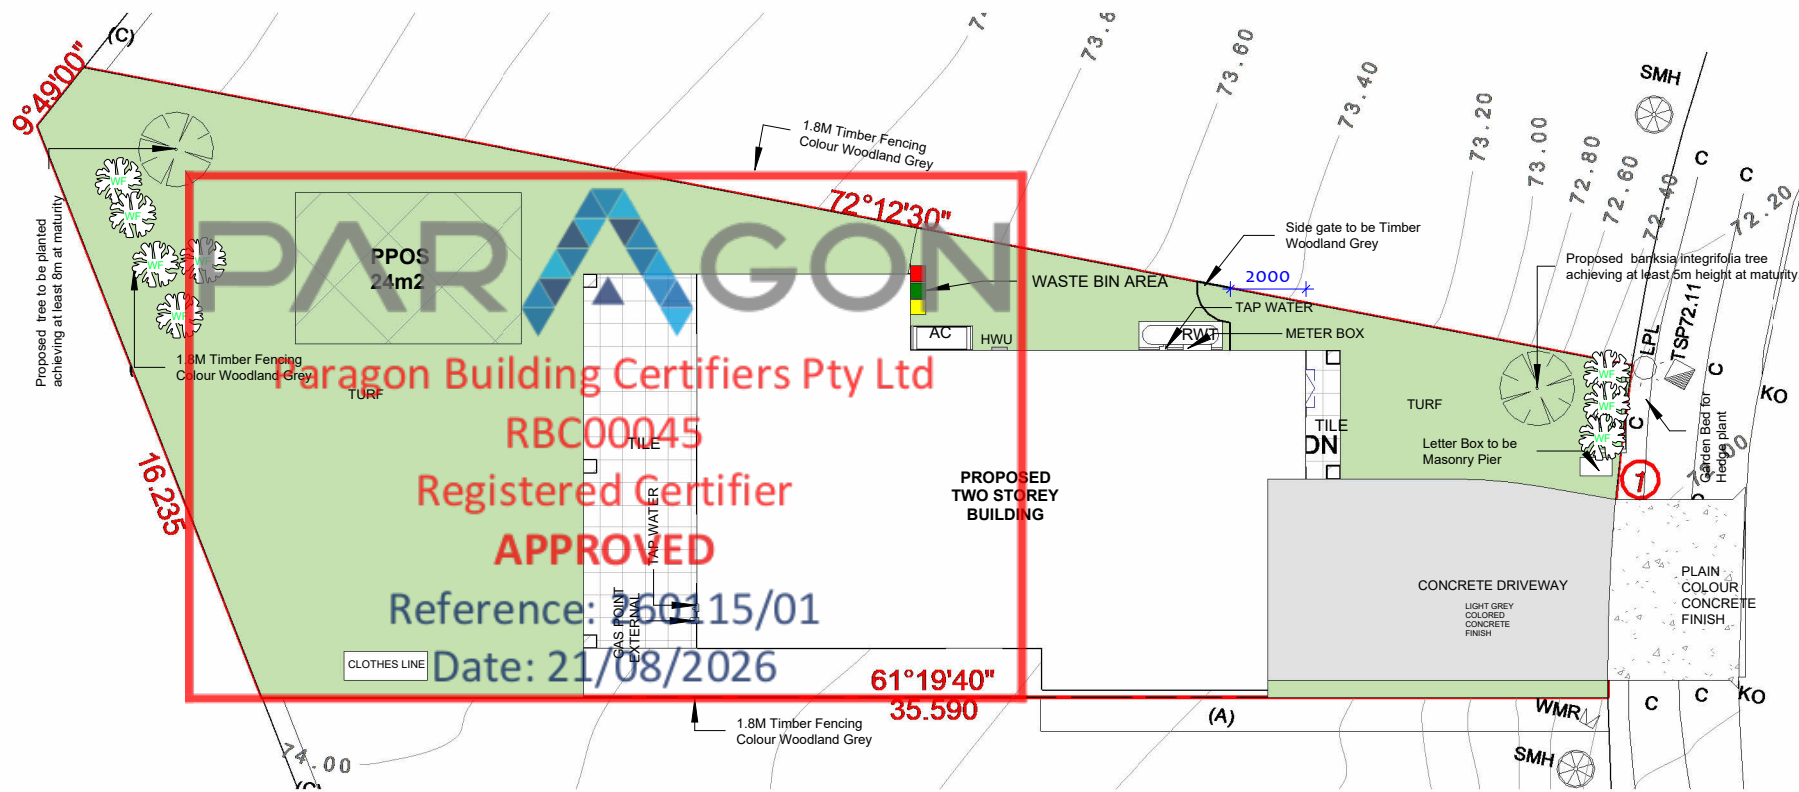

RIDGEWAY DRIVE

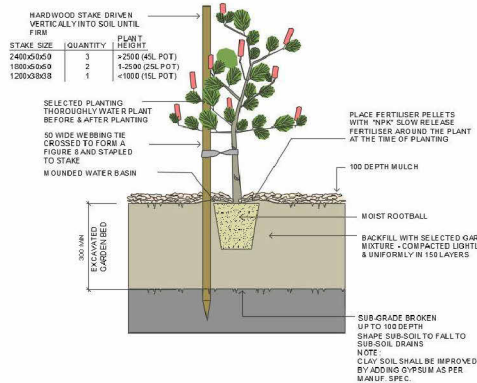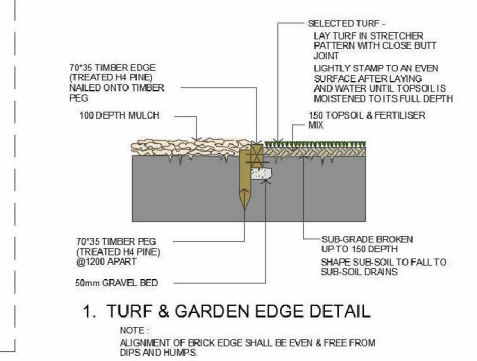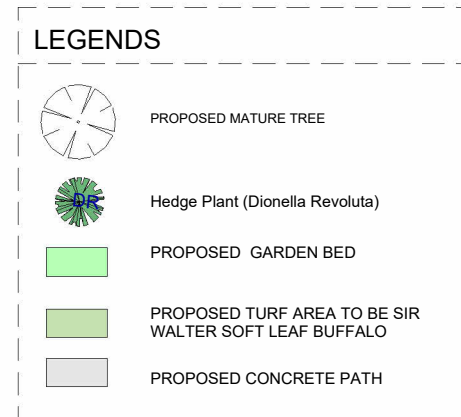

LANDSCAPE PLAN

1 : 200

- GENERAL NOTES:**
- LANDSCAPE CONTRACTOR TO CHECK DA CONDITIONS AND STAMPED LANDSCAPE PLAN
 - BEFORE COMMENCING WORKS TO ENSURE NO ADDITIONS/AMENDMENTS TO PLAN.
 - GARDEN BEDS IN OSD BASIN TO CONSIST OF NON FLOATABLE DECORATIVE GRAVEL.
 - REFER TO HYDRAULICS ENGINEERS PLAN FOR OSD DETAILS/FINAL LEVELS.
 - MULCHED PLANTING BEDS TO BE A MINIMUM DEPTH OF 75mm AS SELECTED.
 - CONTRACTOR'S RESPONSIBILITY TO CHECK AND ADJUST SOIL pH AS REQUIRED.
 - PROVIDE TIMBER EDGE AS A MINIMUM BENEATH FENCING/GATES TO DEFINE TURF AND GARDEN BEDS/PATHWAYS.EDGING TO BE PROVIDED TO ALL AREAS WHERE DIFFERING MATERIALS MEET I.e TURF/GARDEN,TURF/GRAVEL PATH ETC.
 - WEED MAT BENEATH GRAVEL GRAVEL PATHWAYS REQUIRED TO LIMIT MUD TRACKING.
 - PREMIUM ORGANIC GARDEN MIX TO BE USED.
 - ALL PLANTS TO BE HEALTHY AND VIGOROUS.
 - CONTRACTOR TO MAKE GOOD TURF ON NATURE STRIP POST CONSTRUCTION
 - CONTRACTOR TO MAKE GOOD TURF ON NATURE STRIP POST CONSTRUCTION.
 - DO NOT SCALE ARCHITECTURAL SETOUT FROM LANDSCAPE DRAWING.
 - EXISTING TREE SPREAD APPROXIMATE ONLY.REFER TO TREE REPORT WHEN APPLICABLE.
 - SITE SURVEY PROVIDED BY OTHERS.
 - BUFFALO TURF PREFERRED OVER KIKUYU.

LANDSCAPE BASIX NOTE:
THE APPLICANT MUST PLANT INDIGENEOUS OR LOW WATER USE SPECIES OF VEGETATION THROUGHOUT 15 SQM OF THE SITE.

NOTE :BUILDER RESERVES THE RIGHT NOT TO UNDERTAKE NOR SUPPLY CERTIFICATE FOR OCCUPATION CERTIFICATE.
NOTE : TO AID COMPLIANCE WITH BASIX LEGISLATION,PLANTS (WHERE APPLICABLE) HAVE BEEN SELECTED FROM THE LOCAL CITY COUNCIL/SHIRE PLANT LISTS.
NOTE: LOCATION OF SEWER MAINS/LINES, WATER PIPES, UNDERGROUND ELECTRICITY AND OTHER SERVICES MUST BE OBTAINED PRIOR TO COMMENCEMENT OF ANY WORK ON SITE.

CONTRACTORS NOTE : CALCULATED ARES DETERMINED BY CAD AND HAVE BEEN ROUNDED UP FOR USE AS A GUIDE ONLY ALLOW STANDARD PERCENTAGE FOR CUTTING AND WASTAGE .CONFIRM DIMENSIONS AND NUMBERS PRIOR TO QUOTING/ORDERING.

PLANT SCHEDULE

Genus	Common Name	Qty	Pot size	Height	width
Trees					
Backhousia myrtifolia	Grey Myrtle	1	45L	6-10m	Dense feature tree with, green glossy foliage. Greenish yellow flowers in small terminal clusters.
Shrubs					
Bursaria Spinosa Var Sppinosa	Blackthorn ,Boxthorn	8	140mm	1.5m	Thorny, wiry branches. Leaf size and shape vary 's with age. Small, white fragrant flowers.
Dodonea Visco ssp. Cuneata	Wedge-Leaf Hop Bush	6	140mm	1m	Compact growth. Sticky leaves taper to sharp point. Green fruit turns red and purple
Indigofera Australis	Native Indigo	5	140mm	1m	Slender, erect. Pink to lilac pea flowers, numerous along stems.
Hedgeing & screening Plants					
Acmena smithii 'Cherry Surprise'	Lilly Pilly Cherry Surprise PBR	10	140mm	3m	It has attractive small dense green foliage that provides a continuous flush of cherry-red new growth nearly all year round. Small white starry flowers bloom in summer.

LANDSCAPE AREA	
FRONT AREA	51.0 m ²
BACKYARD AREA	180 m ²




Bursaria spinosa
var spinosa
Blackthorn, Boxthorn
Type: Shrub. Description: Thorny, wiry branches. Leaf size and shape vary's with age. Small, white fragrant flowers. *Height:* Medium. *Flowers:* Jan-April. *Propagation:* sow seed. *Prune:* after flowering, only to maintain shape.



Dodonea viscosa ssp.
Cuneata
Wedge-leaf Hop Bush
Type: Shrub. Description: Compact growth. Sticky leaves taper to sharp point. Green fruit turns red and purple. *Height:* 1m. *Flowers:* Spring. *Propagation:* from seed or take cutting in Spring and Summer. *Prune:* minimally.



Indigofera australis
Native Indigo
Type: Shrub. Description: Slender, erect. Pink to lilac pea flowers, numerous along stems. *Height:* 1m. *Flowers:* Spring. *Propagation:* from seed, early to mid Summer. *Prune:* trim lightly after flowering.

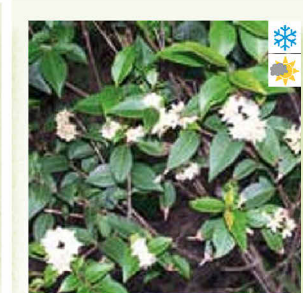

Backhousia myrtifolia
Grey Myrtle
Type: Tree. Description: Dense feature tree with, green glossy foliage. Greenish yellow flowers in small terminal clusters. *Height:* 6-10m. *Flowers:* Nov-Dec. *Propagation:* sow seed in Spring. *Prune:* minimally.


REV	DATE	DESCRIPTION	BY
5	31-07-2026	CC ISSUE	
4	29-06-2026	RFI 3 ISSUE	
3	16-06-2026	RFI 2 ISSUE	
2	26-05-2026	RFI ISSUE	
1	22-04-2026	DA ISSUE	

THIS DRAWING IS THE EXCLUSIVE PROPERTY OF THE DEVELOPER & THE REPRODUCTION OF ANY PART WITHOUT THE PRIOR WRITTEN CONSENT OF THE DEVELOPER IS A VIOLATION OF APPLICABLE LAWS. IN NO EVENT SHALL THE DEVELOPER BE HELD LIABLE FOR SPECIAL COLLATERAL, INCIDENTAL OR CONSEQUENTIAL LIABILITY IN CONNECTION WITH THE USE OF THIS DIGITAL DATA ONCE RELEASED FROM THE DEVELOPER'S OFFICE. THIS DRAWING IS TO BE READ & UNDERSTOOD IN CONJUNCTION WITH THE STRUCTURAL, MECHANICAL, ELECTRICAL & / OR ANY OTHER CONSULTANT'S DOCUMENTATION AS MAY BE APPLICABLE TO THE PROJECT PRIOR TO THE START OF ANY WORKS AND FOR ITS DURATION.

PROJECT:
Residential Dwelling

LOT 1008 IN DP 1306994
LOCATED AT No.16 Ridgeway Drive Orchard Hills NSW.

DRAWING TITLE:
LANDSCAPE PLAN

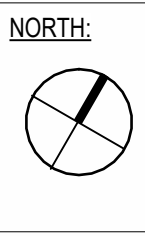

LOT NO:	DATE:	SCALE:	DRAWING No:	REV:
1008	11-08-2026	1 : 200	CC.15	5
DRAWN BY:	CHECKED BY:	CLIENT NAME:	ISSUED BY:	
AS	RH	Saggita Reddy		
DRAFTED BY:	SL			

CC ISSUE

Single Dwelling

Certificate number: 1835426S_02

This certificate confirms that the proposed development will meet the NSW government's requirements for sustainability, as built in accordance with the commitments set out below. Terms used in the certificate, or in the commitments, have the meaning given by the document entitled "BASIX Definitions" dated 10/09/2020 published by the Department. This document is available at www.planningportal.nsw.gov.au/definitions

Secretary
Date of issue: Thursday, 16 April 2026
To be valid, this certificate must be submitted with a development application or lodged with a complying development certificate application within the time frame of the date of issue.



Project summary			
Project name	16 RIDGEWAY DRIVE ORCHARD HILLS, 02		
Street address	16 RIDGEWAY Drive ORCHARD HILLS 2748		
Local Government Area	Penrith City Council		
Plan type and plan number	Deposited Plan DP1306994		
Lot no.	1008		
Section no.	-		
Project type	dwelling house (detached)		
No. of bedrooms	5		
Project score			
Water	40	Target 40	
Thermal Performance	Pass	Target Pass	
Energy	71	Target 70	
Materials	46	n/a	

Certificate Prepared by	
RBC00045	
Name / Company Name: HOMESALE PTY LTD.	
ABN (if applicable): 76336721180	

Paragon Building Certifiers Pty Ltd

Registered Certifier
APPROVED

Reference: 260115/01
Date: 21/08/2026

Description of project

Project address		Assessor details and thermal loads	
Project name	16 RIDGEWAY DRIVE ORCHARD HILLS, 02	NatHERS assessor number	n/a
Street address	16 RIDGEWAY Drive ORCHARD HILLS 2748	NatHERS certificate number	n/a
Local Government Area	Penrith City Council	Climate zone	n/a
Plan type and plan number	Deposited Plan DP1306994	Area adjusted cooling load (MJ/ m² year)	n/a
Lot no.	1008	Area adjusted heating load (MJ/ m² year)	n/a
Section no.	-		
Project type		Project score	
Project type	dwelling house (detached)		
No. of bedrooms	5		
Site details			
Site area (m²)	491		
Roof area (m²)	220		
Conditioned floor area (m²)	194.0		
Unconditioned floor area (m²)	15.0		
Total area of garden and lawn (m²)	228		
Roof area of the existing dwelling (m²)	0		

Water	40	Target 40
Thermal Performance	Pass	Target Pass
Energy	71	Target 70
Materials	46	Target n/a

Thermal Performance and Materials commitments				Show on DA plans	Show on CC/CDC plans & specs	Certifier check
Do-it-yourself Method						
General features						
The dwelling must be a Class 1 dwelling according to the National Construction Code, and must not have more than 2 storeys.				✓	✓	✓
The conditioned floor area of the dwelling must not exceed 300 square metres.				✓	✓	✓
The dwelling must not contain open mezzanine area exceeding 25 square metres.				✓	✓	✓
The dwelling must not contain third level habitable attic room.				✓	✓	✓
Floor, walls and ceiling/roof						
The applicant must construct the floor(s), walls and ceiling/roof of the dwelling in accordance with the specifications listed in the table below.				✓	✓	✓
The applicant must adopt one of the options listed in the table below to address thermal bridging in metal framed floor(s), walls and ceiling/roof of the dwelling.				✓	✓	✓
The applicant must show through receipts that the materials purchased for construction are consistent with the specifications listed in the tables below.						✓
Construction	Area - m²	Additional insulation required	Options to address thermal bridging	Other specifications		
foot - concrete slab on ground, walls pool slab, walls pool slab	30	not specified	nil			
garage floor - concrete slab on ground, walls pool slab	30	none	nil			
external wall: brick veneer; frame: timber - H2 treated softwood.	235	2.84 (or 3.50 including construction)/fibreglass batts or nil	nil	wall colour: Medium (solar absorptance 0.48-0.7)		

Construction	Area - m ²	Additional insulation required	Options to address thermal bridging	Other specifications
external wall: framed (solid or reconstituted timber weatherboard); frame: timber - H2 treated softwood	19.5	3.00 (or 3.50 including cavity-chim/thergless batts or roll)	nil	wall colour: Medium (solar absorptance 0.48-0.7)
internal wall shared with garage; frame: timber - H2 treated softwood	24.5	none	nil	
internal wall: plasterboard; frame: timber - H2 treated softwood	188	none	nil	
ceiling and roof - flat ceiling / pitched roof; frame: metal roof, timber - H2 treated softwood	220	ceiling: 5 (up); roof: foil backed blanket; ceiling: foil backed blanket; roof: foil backed blanket	nil	roof space ventilation: wind-driven ventilator(s) + eave vents, roof colour: medium (solar absorptance 0.48-0.59); 0.5 to < 1.0% of ceiling area unventilated
Notes - Insulation specified in this Certificate must be installed in accordance with the ABCB Housing Provisions (Part 13.2.2) of the National Construction Code.				
Note - If the additional ceiling insulation listed in the table above is greater than R3.0, refer to the ABCB Housing Provisions (Part 13.2.3 (b)) of the National Construction Code.				
Note - In some climate zones, insulation should be installed with due consideration of condensation and associated interaction with adjoining building materials.				
Note - Thermal breaks must be installed in metal framed walls and applicable roofs in accordance with the ABCB Housing Provisions of the National Construction Code.				

Thermal Performance and Materials commitments				Show on DA plans	Show on CC/CDC plans & specs	Certifier check
Glazed windows, doors and skylights						
The applicant must install the windows, glazed doors and shading devices described in the table below, in accordance with the specifications listed in the table. Relevant overshadowing specifications must be satisfied for each glazed window and door:				✓	✓	✓
The dwelling may have 1 skylight (<0.7 square metres) which is not listed in the table.				✓	✓	✓
The following requirements must also be satisfied in relation to each window and glazed door:				✓	✓	✓
• The applicant must install windows and glazed doors in accordance with the height and width, frame and glazing types listed in the table.				✓	✓	✓
• Each window and glazed door must have a U-value no greater than that listed and a Solar Heat Gain Coefficient (SHGC) within the range listed. Total system U-values and SHGC must be calculated in accordance with National Fire Protection Rating Council (NFRC) conditions.				✓	✓	✓
The applicant must install the skylights described in the table below, in accordance with the specifications listed in the table. Total skylight area must not exceed 3 square metres (the 3 square metre limit does not include the optional additional skylight of less than 0.7 square metres that does not have to be listed in the table).				✓	✓	✓
Glazed window/door no.	Maximum height (mm)	Maximum width (mm)	Frame and glass specification	Shading device (dimension within 10%)	Overshadowing	
North-East facing						
GW1	1800.00	1000.30	aluminium, single glazed (U-value: <=6.0, SHGC: 0.74 - 0.90)	solid overhang 300 mm, 100 mm above head of window or glazed door	not overshadowed	
FW1	950.00	1500.30	aluminium, single glazed (U-value: <=6.0, SHGC: 0.74 - 0.90)	eave 450 mm, 100 mm above head of window or glazed door	not overshadowed	
SD2	2300.00	2400.30	aluminium, single glazed (U-value: <=6.0, SHGC: 0.74 - 0.90)	eave 1350 mm, 100 mm above head of window or glazed door	not overshadowed	
South-East facing						

Glazed window/door no.	Maximum height (mm)	Maximum width (mm)	Frame and glass specification	Shading device (dimensional within 10%)	Overshadowing
GW5	600.00	1800.00	aluminium, single glazed (U-value: <=6.0, SHGC: 0.74 - 0.90)	eave 450 mm, 4000 mm above head of window or glazed door	not overshadowed
GW6	600.00	900.00	aluminium, single glazed (U-value: <=6.0, SHGC: 0.74 - 0.90)	eave 450 mm, 4000 mm above head of window or glazed door	not overshadowed
GW7	1400.00	1500.00	aluminium, single glazed (U-value: <=6.0, SHGC: 0.74 - 0.90)	eave 450 mm, 3137 mm above head of window or glazed door	not overshadowed
FW7	800.00	1200.00	aluminium, single glazed (U-value: <=6.0, SHGC: 0.74 - 0.90)	eave 450 mm, 50 mm above head of window or glazed door	not overshadowed
FW8	800.00	2200.00	aluminium, single glazed (U-value: <=6.0, SHGC: 0.74 - 0.90)	eave 450 mm, 50 mm above head of window or glazed door	not overshadowed
South-West facing					
GW4	1400.00	1800.00	aluminium, single glazed (U-value: <=6.0, SHGC: 0.74 - 0.90)	verandah 3450 mm, 1600 mm above base of window or glazed door	not overshadowed
FW5	1450.00	1500.00	aluminium, single glazed (U-value: <=6.0, SHGC: 0.74 - 0.90)	eave 450 mm, 50 mm above head of window or glazed door	not overshadowed
FW6	1450.00	1500.00	aluminium, single glazed (U-value: <=6.0, SHGC: 0.74 - 0.90)	eave 450 mm, 50 mm above head of window or glazed door	not overshadowed
SD1	2300.00	2400.00	aluminium, single glazed (U-value: <=6.0, SHGC: 0.74 - 0.90)	verandah 3450 mm, 2600 mm above base of window or glazed door	not overshadowed
North-West facing					
GW2	800.00	800.00	aluminium, single glazed (U-value: <=6.0, SHGC: 0.74 - 0.90)	eave 450 mm, 3137 mm above head of window or glazed door	not overshadowed

Energy Commitments				Show on DA plans	Show on CC/CDC plans & specs	Certifier check
Hot water						
The applicant must install the following hot water system in the development, or a system with a higher energy rating: gas instantaneous with a performance of 5 stars.				✓	✓	✓
Cooling system						
The applicant must install the following cooling system, or a system with a higher energy rating, in at least 1 living area: 3-phase air conditioning. Energy rating: EER 3.0 - 3.5					✓	✓
The applicant must install the following cooling system, or a system with a higher energy rating, in at least 1 bedroom: 3-phase air conditioning. Energy rating: EER 3.0 - 3.5					✓	✓
Heating system						
The applicant must install the following heating system, or a system with a higher energy rating, in at least 1 living area: 3-phase air conditioning. Energy rating: EER 3.0 - 3.5					✓	✓
The applicant must install the following heating system, or a system with a higher energy rating, in at least 1 bedroom: 3-phase air conditioning. Energy rating: EER 3.0 - 3.5					✓	✓
Ventilation						
The applicant must install the following exhaust systems in the development:						
At least 1 Bathroom: no mechanical ventilation (ie. natural). Operation control: n/a					✓	✓
Kitchen: individual fan, ducted to facade or roof. Operation control: manual switch on/off					✓	✓
Laundry: natural ventilation only, or no laundry. Operation control: n/a					✓	✓
Artificial lighting						
The applicant must ensure that a minimum of 80% of light fixtures are fitted with Fluorescent, compact fluorescent, or light-emitting-diode (LED) lamps.					✓	✓
Natural lighting						
The applicant must install a window and/or skylight in 4 bathroom(s)/suite(s) in the development for natural lighting.				✓	✓	✓

Energy Commitments				Show on DA plans	Show on CC/CDC plans & specs	Certifier check
Other						
The applicant must install a gas cooktop & electric oven in the kitchen of the dwelling.					✓	
The applicant must install a fixed outdoor clothes drying line as part of the development.					✓	

Schedule of BASIX commitments

The commitments set out below regulate how the proposed development is to be carried out. It is a condition of any development consent granted, or complying development certificate issued, for the proposed development, that BASIX commitments be complied with.

Water Commitments				Show on DA plans	Show on CC/CDC plans & specs	Certifier check
Fixtures						
The applicant must install showerheads with a minimum rating of 4 star (> 4.5 but <= 6 L/min per spray force and/or coverage tests) in all showers in the development.					✓	✓
The applicant must install a toilet flushing system with a minimum rating of 4 star in each toilet in the development.					✓	✓
The applicant must install taps with a minimum rating of 4 star in the kitchen in the development.					✓	✓
The applicant must install basin taps with a minimum rating of 4 star in each bathroom in the development.					✓	✓
Alternative water						
Rainwater tank						
The applicant must install a rainwater tank of at least 1500 litres on the site. This rainwater tank must meet, and be installed in accordance with, the requirements of all applicable regulatory authorities.				✓	✓	✓
The applicant must configure the rainwater tank to collect rain runoff from at least 220 square metres of the roof area of the development (excluding the area of the roof which drains to any stormwater tank or private dam).					✓	✓
The applicant must connect the rainwater tank to:					✓	✓
• the cold water tap that supplies each clothes washer in the development					✓	✓
• at least one outdoor tap in the development (Note: NSW Health does not recommend that rainwater be used for human consumption in areas with potable water supply.)					✓	✓

Thermal Performance and Materials commitments				Show on DA plans	Show on CC/CDC plans & specs	Certifier check
Ceiling fans						
The applicant must install at least one ceiling fan in at least one daytime habitable space, such as living room.				✓	✓	✓
• The minimum number and diameter of ceiling fans in a daytime habitable space must be installed in accordance with the ABCB Housing Provisions (Part 13.5.2) of the National Construction Code				✓	✓	✓

Glazed window/door no.	Maximum height (mm)	Maximum width (mm)	Frame and glass specification	Shading device (dimensional within 10%)	Overshadowing	
GW3	1500.00	1800.00	aluminium, single glazed (U-value: <=6.0, SHGC: 0.74 - 0.90)	eave 450 mm, 3137 mm above head of window or glazed door	not overshadowed	
FW2	800.00	1500.00	aluminium, single glazed (U-value: <=6.0, SHGC: 0.74 - 0.90)	eave 450 mm, 50 mm above head of window or glazed door	not overshadowed	
FW3	2050.00	1200.00	aluminium, single glazed (U-value: <=6.0, SHGC: 0.74 - 0.90)	eave 450 mm, 50 mm above head of window or glazed door	not overshadowed	
FW4	600.00	800.00	aluminium, single glazed (U-value: <=6.0, SHGC: 0.74 - 0.90)	eave 450 mm, 50 mm above head of window or glazed door	not overshadowed	

Legend	
In these commitments, "applicant" means the person carrying out the development.	
Commitments identified with a ✓ in the "Show on DA plans" column must be shown on the plans accompanying the development application for the proposed development (if a development application is to be lodged for the proposed development).	
Commitments identified with a ✓ in the "Show on CC/CDC plans and specs" column must be shown in the plans and specifications accompanying the application for a construction certificate / complying development certificate for the proposed development.	
Commitments identified with a ✓ in the "Certifier check" column must be certified by a certifying authority as having been fulfilled, before a final occupation certificate (either interim or final) for the development may be issued.	

REV	DATE	DESCRIPTION	BY
5	31-07-2026	CC ISSUE	
4	29-06-2026	RFI 3 ISSUE	
3	16-06-2026	RFI 2 ISSUE	
2	26-05-2026	RFI ISSUE	
1	22-04-2026	DA ISSUE	




RUBY HOMES

THIS DRAWING IS THE EXCLUSIVE PROPERTY OF THE DEVELOPER & THE REPRODUCTION OF ANY PART WITHOUT THE PRIOR WRITTEN CONSENT OF THE DEVELOPER IS A VIOLATION OF APPLICABLE LAWS. IN NO EVENT SHALL THE DEVELOPER BE HELD LIABLE FOR SPECIAL COLLATERAL, INCIDENTAL OR CONSEQUENTIAL LIABILITY IN CONNECTION WITH THE USE OF THIS DIGITAL DATA ONCE RELEASED FROM THE DEVELOPER'S OFFICE. THIS DRAWING IS TO BE READ & UNDERSTOOD IN CONJUNCTION WITH THE STRUCTURAL, MECHANICAL, ELECTRICAL & / OR ANY OTHER CONSULTANT'S DOCUMENTATION AS MAY BE APPLICABLE TO THE PROJECT PRIOR TO THE START OF ANY WORKS AND FOR ITS DURATION.

PROJECT:
Residential Dwelling

DRAWING TITLE:
BASIX

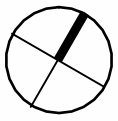NORTH:


LOT NO:
1008

DRAWN BY:
AS

DRAFTED BY:
SL

DATE:
11-08-2026

CHECKED BY:
RH

CLIENT NAME:
Saggita Reddy

SCALE:

DRAWING No:
CC.18

REV:
5

ISSUED BY:

CC ISSUE