

FOR CONSTRUCTION

LOT 342 - 36 PLEIADES STREET AUSTRAL. IN DP 1311926.

PROPOSED CONSTRUCTION OF A TWO STOREY DWELLING



BASIX COMMITMENTS		Certificate number: 1861503S Date of issue: Tuesday, 18 August 2026
WATER		
LANDSCAPE	114m2	
TOILETS	4 STARS	
KITCHEN TAPS	4 STARS	
SHOWER HEADS	5 STAR (>4.5 but <=6 Umin)	
BASIN TAPS	4 STARS	
ALTERNATIVE WATER	1500L RAINWATER TANK	
ROOF WATER TO TANK	155m2	
ALT.WATER USES- TANK	LAUNDRY	
ALT. WATER USES - RETIC	ALL TOILETS + ONE OUTDOOR TAP	
SWIMMING POOL	N/A	
ENERGY		
HOT WATER	GAS INSTANTANEOUS - 6 STAR	
AIR-CON (HEATING)	3 PHASE DUCTED - EER 3.5-4.0	
AIR-CON (COOLING)	3 PHASE DUCTED - EER 3.5-4.0	
VENTILATION - BATHROOM	NONE/ NATURAL VENTILATION	
VENTILATION - KITCHEN	DUCTED - MANUAL SWITCH	
VENTILATION - LAUNDRY	NONE/ NATURAL VENTILATION	
PV SYSTEM	N/A	
COOKTOP	GAS	
OVEN	ELECTRIC	
CLOTHES DRYING	OUTDOOR CLOTHESLINE	
LIGHTING	DEDICATED LED	

GENERAL LEGEND	
AC	AIR CONDITIONING UNIT
AL	POWDERCOATED ALUMINIUM DOOR/WINDOW
BAL	Sydney Wide Certifiers Pty Ltd
BG	Complying Development Certificate
BR1, BR2, etc.	Reference SWC262604/01
CAP	Date: 21/08/2026
CD1, CD2, etc.	Sandres Markhani
CONC.	BDC05035
CONC.	CONCRETE FLOOR
CR1	CONCRETE ROOF TILES
CR1, CR2, etc.	CEMENT RENDER TYPE/ COLOUR
DPIS	DOWN PIPE
DW	DISH WASHER
ED	ENTRY DOOR
F	FRIDGE
FAS	FASCIA
FET	FEATURE TILE
FT, FT1, FT2, etc.	FLOOR TILES
FW	FLOOR WASTE
GD	GARAGE DOOR
GUT	GUTTER
HWU	HOT WATER UNIT
HYB	HYBRID FLOOR
L	LINEN
MR	METAL ROOF
MW	MICROWAVE OVEN
NGL	NATURAL GROUND LEVEL
OBS	OBSCURED GLASS
P	PANTRY
R	ROBE
RL	REDUCED LEVEL
RWH	RAIN WATER HEAD
RWT	RAIN WATER TANK
S	STORAGE
TOW	TOP OF WALL
TL	TIMBER LAMINATE
WC	WATER CLOSET
WM	WASHING MACHINE
SD	SMOKE DETECTOR

Sheet List				
Sheet No.	Sheet Name	Drawn By	Current Revision Date	Current Revision
CDC.01	COVER SHEET	AS	20-08-2026	CDC ISSUE
CDC.02A	GENERAL NOTES	AS	25-06-2026	CDC ISSUE
CDC.02B	GENERAL NOTES	AS	25-06-2026	CDC ISSUE
CDC.03	LOCATION PLAN AND SITE PLAN	AS	25-06-2026	CDC ISSUE
CDC.04	SITE ANALYSIS AND SEDIMENT CONTROL	AS	25-06-2026	CDC ISSUE
CDC.05	GROUND FLOOR PLAN	AS	20-08-2026	CDC ISSUE
CDC.06	FIRST FLOOR LEVEL	AS	25-06-2026	CDC ISSUE
CDC.07	ROOF PLAN	AS	25-06-2026	CDC ISSUE

Sheet List				
Sheet No.	Sheet Name	Drawn By	Current Revision Date	Current Revision
CDC.08	ELEVATION 01	AS	25-06-2026	CDC ISSUE
CDC.09	ELEVATION 02	AS	25-06-2026	CDC ISSUE
CDC.10	SECTIONS	AS	25-06-2026	CDC ISSUE
CDC.11	FLOOR AREA PLAN	AS	25-06-2026	CDC ISSUE
CDC.12	RENTABLE AREA PLAN	AS	25-06-2026	CDC ISSUE
CDC.14	COLOR SCHEDULE	AS	25-06-2026	CDC ISSUE
CDC.15	LANDSCAPE PLAN	AS	25-06-2026	CDC ISSUE
CDC.16	WATERPROOFING PLAN	AS	25-06-2026	CDC ISSUE

8	20-08-2026	Wardrobe added to G.bed	
7	25-06-2026	230 Brick wall in Garage	
6	30-03-2026	Shower in GF Bath-Ek	
5	24-03-2026	Bed2 made 3600, Robe position changed, Store under stairs-Ekta	
4	23-03-2026	Bathtub added takin space from M.Bed and WIR. Linen Moved to Laundry - Ekta	
3	19-03-2026	Bank Set 1500mm setback as per BEP	
REV	DATE	DESCRIPTION	BY



THIS DRAWING IS THE EXCLUSIVE PROPERTY OF THE DEVELOPER & THE REPRODUCTION OF ANY PART WITHOUT THE PRIOR WRITTEN CONSENT OF THE DEVELOPER IS A VIOLATION OF APPLICABLE LAWS. IN NO EVENT SHALL THE DEVELOPER BE HELD LIABLE FOR SPECIAL, COLLATERAL, INCIDENTAL OR CONSEQUENTIAL LIABILITY IN CONNECTION WITH THE USE OF THIS DIGITAL DATA ONCE RELEASED FROM THE DEVELOPERS OFFICE. THIS DRAWING IS TO BE READ & UNDERSTOOD IN CONJUNCTION WITH THE STRUCTURAL, MECHANICAL, ELECTRICAL &/OR ANY OTHER CONSULTANTS' DOCUMENTATION AS MAY BE APPLICABLE TO THE PROJECT PRIOR TO THE START OF ANY WORKS AND FOR ITS DURATION.

PROJECT:
Lot 342 36 PLEIADES STREET
36 PLEIADES STREET AUSTRAL

DRAWING TITLE:
COVER SHEET

NORTH:


<u>NORTH:</u>		DATE:	SCALE:	DRAWING No:	REV:
LOT NO:	342	20-08-2026			8
DRAWN BY:	CHECKED BY:	As indicated	CDC.01	ISSUED BY:	
AS	RH				
DRAFTED BY:	CLIENT NAME:				
ID	Umesh Bhandari and Meena Khattri Bhandari				

BUILDING SPECIFICATIONS

National Construction Code – Volume 2, Amendment 1 – Building Code of Australia 2022 & Housing Provisions Standard 2022

SITE PREPARATION

- PART 3.1 OF THE NCC VOLUME 2, AMENDMENT 1 - BUILDING CODE OF AUSTRALIA 2022 & HOUSING PROVISIONS STANDARD 2022.

EARTHWORKS

- TO BE CARRIED OUT IN ACCORDANCE WITH THE REQUIREMENTS OF THE ENVIRONMENTAL PLANNING & ASSESSMENT ACT 1979 AND DEVELOPMENT CONSENT CONDITIONS
- PART 3.2 OF THE NCC VOLUME 2, AMENDMENT 1 - BUILDING CODE OF AUSTRALIA 2022 & HOUSING PROVISIONS STANDARD 2022.
- AS 4678:2002 - EARTH-RETAINING STRUCTURES

DRAINAGE

- PART 3.3 OF THE NCC VOLUME 2, AMENDMENT 1 - BUILDING CODE OF AUSTRALIA 2022 & HOUSING PROVISIONS STANDARD 2022.
- AS/NZS 3500.1:2021 - PLUMBING & DRAINAGE - WATER SERVICES
- AS/NZS 3500.2:2021 - PLUMBING & DRAINAGE - SANITARY PLUMBING & DRAINAGE
- AS/NZS 3500.3:2021 - PLUMBING & DRAINAGE STORMWATER DRAINAGE
- AS/NZS 3500.4:2021 - PLUMBING & DRAINAGE - HEATED WATER SERVICES

STRUCTURAL WORK

- Part 2.2 OF THE NCC VOLUME 2, AMENDMENT 1 - BUILDING CODE OF AUSTRALIA 2022 & HOUSING PROVISIONS STANDARD 2022.
- AS 4100:2020 - STEEL STRUCTURES CODES
- AS/NZS 1170.0:2002 - GENERAL PRINCIPLES
- AS/NZS 1170.1:2002 - PARTS 1 PERMANENT, IMPOSED AND OTHER ACTIONS
- AS/NZS 1170.2:2021 - PART 2 WIND ACTIONS
- AS 3700:2018 - SAA MASONRY CODE
- AS 1684.3:2021 - RESIDENTIAL TIMBER FRAMED CONSTRUCTION

FOOTINGS & SLABS

- PART 4 OF THE NCC VOLUME 2, AMENDMENT 1 - BUILDING CODE OF AUSTRALIA 2022 & HOUSING PROVISIONS STANDARD 2022.
- AS 2159:2009 - PILING - DESIGN & INSTALLATION
- AS 2870:2011 - RESIDENTIAL SLABS & FOOTINGS
- AS 3600:2018 - CONCRETE STRUCTURES

MASONRY

- PART 5 OF THE NCC VOLUME 2, AMENDMENT 1 - BUILDING CODE OF AUSTRALIA 2022 & HOUSING PROVISIONS STANDARD 2022.
- AS 3700:2018 - MASONRY STRUCTURES

FRAMING

- PART 6 OF THE NCC VOLUME 2, AMENDMENT 1 - BUILDING CODE OF AUSTRALIA 2022 & HOUSING PROVISIONS STANDARD 2022.
- AS 1684.2:2021 - RESIDENTIAL TIMBER-FRAMED CONSTRUCTION - NON- CYCLONIC AREAS
- AS 1720.1:2010 - TIMBER STRUCTURES - DESIGN METHODS
- AS 4100:2020 - STEEL STRUCTURES
- AS 3660.1:2014 - TERMITE MANAGEMENT SYSTEM

ROOF & WALL CLADDING

- PART 7 OF THE NCC VOLUME 2, AMENDMENT 1 - BUILDING CODE OF AUSTRALIA 2022 & HOUSING PROVISIONS STANDARD 2022.
- AS 1273:1991 - UNPLASTICIZED PVC (UPVC) DOWNPIPES & FITTINGS FOR RAINWATER
- AS 1562.1:2018 - DESIGN & INSTALLATION OF SHEET ROOF & WALL CLADDING - METAL
- AS/NZS 1562.3:2005 - DESIGN & INSTALLATION OF SHEET ROOF & WALL CLADDING - PLASTIC
- AS 2049:2002 - ROOF TILES
- AS 2050:2018 - INSTALLATION OF ROOF TILES
- AS 4285:2019 - ROOFLIGHTS

GLAZING

- PART 8 OF THE NCC VOLUME 2, AMENDMENT 1 - BUILDING CODE OF AUSTRALIA 2022 & HOUSING PROVISIONS STANDARD 2022.
- AS 1288:2021 - GLASS IN BUILDINGS - SELECTION & INSTALLATION
- AS 2047:2014 - WINDOWS & EXTERNAL GLAZED DOORS IN BUILDINGS
- AS/NZS 2208:1996 - SAFETY GLAZING MATERIALS IN BUILDINGS

FIRE SAFETY

- PART 9 OF THE NCC VOLUME 2, AMENDMENT 1 - BUILDING CODE OF AUSTRALIA 2022 & HOUSING PROVISIONS STANDARD 2022.
- AS 3786:2014 - SMOKE ALARMS USING SCATTERED LIGHT, TRANSMITTED LIGHT OR IONIZATION

HEALTH & AMENITY

- PART 10 OF THE NCC VOLUME 2, AMENDMENT 1 - BUILDING CODE OF AUSTRALIA 2022 & HOUSING PROVISIONS STANDARD 2022.
- AS/NZS ISO 717.1:2004 - ACOUSTICS - RATING OF SOUND INSULATION IN BUILDINGS & OF BUILDING ELEMENTS - AIRBORNE SOUND INSULATION
- AS ISO 717.2:2004 - ACOUSTICS - RATING OF SOUND INSULATION IN BUILDINGS & OF BUILDING ELEMENTS - IMPACT SOUND INSULATION
- AS 1668.2:2012 - THE USE OF VENTILATION & AIR CONDITIONING IN BUILDINGS - MECHANICAL VENTILATION IN BUILDINGS
- AS 1668.4:2012 - THE USE OF VENTILATION & AIR CONDITIONING IN BUILDINGS - NATURAL VENTILATION OF BUILDINGS
- AS/NZS 1680.0:2009 - INTERIOR LIGHTING - SAFE MOVEMENT
- AS 3740:2021 - WATERPROOFING OF DOMESTIC WET AREAS
- AS 3000:2018 - ELECTRICAL INSTALLATION
- BCA Part 10.8.1, AS4200.1 & AS4200.2 - PLIABLE BUILDING MEMBRANE INSTALLED.

WATERPROOFING

- PART 10.2 OF THE NCC VOLUME 2, AMENDMENT 1 - BUILDING CODE OF AUSTRALIA 2022 & HOUSING PROVISIONS STANDARD 2022
- AS 3740:2021 - WATERPROOFING TO WET AREA
- AS 4654:2012 - EXTERNAL WET AREAS

SAFE MOVEMENT & ACCESS

- PART 11 OF THE NCC VOLUME 2, AMENDMENT 1 - BUILDING CODE OF AUSTRALIA 2022 & HOUSING PROVISIONS STANDARD 2022.
- AS 1428.1:2009 - DESIGN FOR ACCESS & MOBILITY - GENERAL REQUIREMENTS FOR ACCESS - NEW BUILDING WORK
- AS 1657:2018 - FIXED PLATFORMS, WALKWAYS, STAIRWAYS & LADDERS - DESIGN, CONSTRUCTION & INSTALLATION

HANDRAILS & BALUSTRADE

- PART 11.3.3 OF THE NCC VOLUME 2, AMENDMENT 1 - BUILDING CODE OF AUSTRALIA 2022 & HOUSING PROVISIONS STANDARD 2022.
- PART 11.3.4 OF THE NCC VOLUME 2, AMENDMENT 1 - BUILDING CODE OF AUSTRALIA 2022 & HOUSING PROVISIONS STANDARD 2022.
- PART 11.3.5 OF THE NCC VOLUME 2, AMENDMENT 1 - BUILDING CODE OF AUSTRALIA 2022 & HOUSING PROVISIONS STANDARD 2022.
- AS 1170.1:2002 - BALUSTRADE INSTALLATION ON OPENABLE WINDOW

PROTECTION

- PART 11.3.7 AND 11.3.8 OF THE NCC VOLUME 2, AMENDMENT 1 - BUILDING CODE OF AUSTRALIA 2022 & HOUSING PROVISIONS STANDARD 2022.

ENERGY EFFICIENCY

- PART 13 OF THE NCC VOLUME 2, AMENDMENT 1 - BUILDING CODE OF AUSTRALIA 2022 & HOUSING PROVISIONS STANDARD 2022 & BASIX CERTIFICATE.

MECHANICAL VENTILATION

- EXHAUST FROM A BATHROOM, SANITARY COMPARTMENT TO DISCHARGE DIRECTLY TO OUTDOOR AIR WITH MINIMUM FLOW RATE OF 25L/S & MAKE-UP AIR VIA OPENINGS TO AN ADJACENT ROOM WITH A FREE AREA OF 14,000 MM². THIS EXHAUST SYSTEM MUST BE INTERLOCKED WITH LIGHT SWITCH AND INCLUDE RUN-ON TIMER SO THAT THE EXHAUST SYSTEM CONTINUES TO OPERATE FOR 10 MINUTES AFTER THE LIGHT SWITCH IS OFF.
- ANY INSTALLED - KITCHEN RANGEHOOD EXHAUST TO DISCHARGE DIRECTLY OR VIA DUCT TO OUTDOOR AIR WITH MINIMUM FLOW RATE OF 40L/S & MAKE-UP AIR VIA OPENINGS TO AN ADJACENT ROOM WITH A FREE AREA OF 14,000 MM².
- LAUNDRY EXHAUST TO DISCHARGE DIRECTLY OR VIA DUCT TO OUTDOOR AIR WITH MINIMUM FLOW RATE OF 40L/S & MAKE-UP AIR VIA OPENINGS TO AN ADJACENT ROOM WITH A FREE AREA OF 14,000 MM².



REV	DATE	DESCRIPTION	BY
7	25-06-2026	230 Brick wall in Garage	
6	30-03-2026	Shower in GF Bath-Ek	



THIS DRAWING IS THE EXCLUSIVE PROPERTY OF THE DEVELOPER & THE REPRODUCTION OF ANY PART WITHOUT THE PRIOR WRITTEN CONSENT OF THE DEVELOPER IS A VIOLATION OF APPLICABLE LAWS. IN NO EVENT SHALL THE DEVELOPER BE HELD LIABLE FOR SPECIAL, COLLATERAL, INCIDENTAL OR CONSEQUENTIAL LIABILITY IN CONNECTION WITH THE USE OF THIS DIGITAL DATA ONCE RELEASED FROM THE DEVELOPER'S OFFICE. THIS DRAWING IS TO BE READ & UNDERSTOOD IN CONJUNCTION WITH THE STRUCTURAL, MECHANICAL, ELECTRICAL & / OR ANY OTHER CONSULTANT'S DOCUMENTATION AS MAY BE APPLICABLE TO THE PROJECT PRIOR TO THE START OF ANY WORKS AND FOR ITS DURATION.

PROJECT:
Lot 342 36 PLEIADES STREET
36 PLEIADES STREET
AUSTRAL

DRAWING TITLE:
GENERAL NOTES

NORTH:

LOT NO:	DATE:	SCALE:	DRAWING No:	REV:
342	20-08-2026	1 : 2	CDC.02A	7
DRAWN BY:	CHECKED BY:	CLIENT NAME:	ISSUED BY:	
AS	RH	Umesh Bhandari and Meena Khattri Bhandari		
DRAFTED BY:				
AS				

CDC ISSUE

TERMITE SHEET

- TERMITE SHEET EXTENDS THROUGH THE ENTIRE MASONRY LEAF AND IS VISIBLE AT THE FINISHED FACE OF THE WALL.


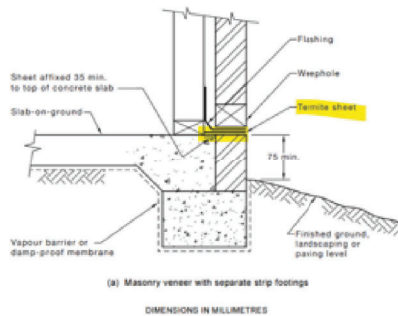


FIGURE 5.5 (in part) TYPICAL SHEET INSTALLATION TO EXTERNAL WALL WITH CONCRETE FLOOR SLAB

DPC FOR BRICKS

DAMP-PROOF COURSE (DPC) TO EXTENDS THROUGH THE ENTIRE MASONRY LEAF AND NEED TO BE VISIBLE AT THE FINISHED FACE OF THE WALL FROM OUTSIDE

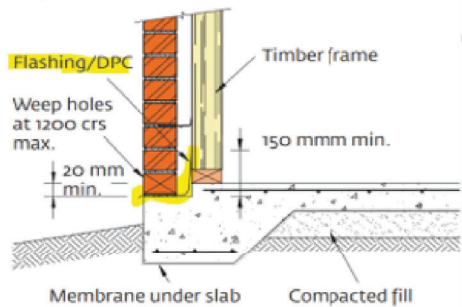

DEMOLITION

- AS 2601-2001 – DEMOLITION WORK

PLANTER BOX

REFER BELOW DETAILS FOR PLANTER BOX.



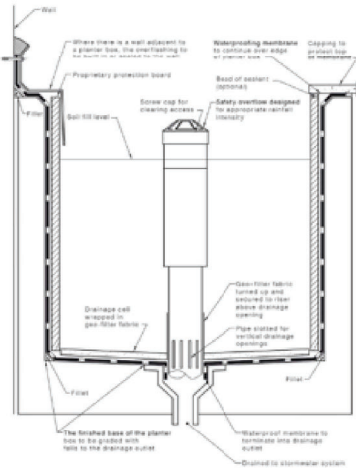


FIGURE 2.17 TYPICAL PLANTER BOX CONSTRUCTION

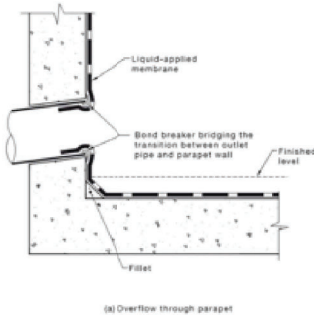

OVERFLOW TO BALCONY:

- SURFACE DRAIN & OVERFLOW TO BALCONY

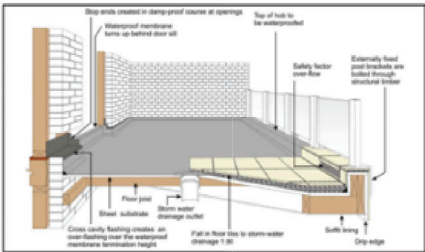

SWIMMING POOL

- PART 12.1.1 (H7D2) OF THE NCC VOLUME 2, AMENDMENT 1 - BUILDING CODE OF AUSTRALIA 2022 & HOUSING PROVISIONS STANDARD 2022
- AS 1926 PART 1-2012 – SWIMMING POOLSAFETY- SAFETY BARRIERS FOR SWIMMING POOLS
- AS 1926 PART 2-2007 - SWIMMING POOL SAFETY- LOCATION OF SAFETY BARRIERS FOR SWIMMING POOLS (INCORPORATING AMENDMENTS 1 AND 2)
- AS 1926 PART 3-2010 – SWIMMING POOL SAFETY- WATER RECIRCULATION SYSTEMS (INCORPORATING AMENDMENT 1)

Sydney Wide Certifiers Pty Ltd
Complying Development Certificate
Reference: SWC262604/01
Date: 21/08/2026
Sandres Markhani BDC05035

REV	DATE	DESCRIPTION	BY
7	25-06-2026	230 Brick wall in Garage	
6	30-03-2026	Shower in GF Bath-Ek	


RUBY HOMES

THIS DRAWING IS THE EXCLUSIVE PROPERTY OF THE DEVELOPER & THE REPRODUCTION OF ANY PART WITHOUT THE PRIOR WRITTEN CONSENT OF THE DEVELOPER IS A VIOLATION OF APPLICABLE LAWS. IN NO EVENT SHALL THE DEVELOPER BE HELD LIABLE FOR SPECIAL COLLATERAL INCIDENTAL OR CONSEQUENTIAL LIABILITY IN CONNECTION WITH THE USE OF THIS DIGITAL DATA ONCE RELEASED FROM THE DEVELOPER'S OFFICE. THIS DRAWING IS TO BE READ & UNDERSTOOD IN CONJUNCTION WITH THE STRUCTURAL, MECHANICAL, ELECTRICAL, &/OR ANY OTHER CONSULTANT'S DOCUMENTATION AS MAY BE APPLICABLE TO THE PROJECT PRIOR TO THE START OF ANY WORKS AND FOR ITS DURATION.


PROJECT:
Lot 342 36 PLEIADES STREET
36 PLEIADES STREET
AUSTRAL

DRAWING TITLE:
GENERAL NOTES

CDC ISSUE					
LOT NO:	DATE:	SCALE:	DRAWING No.	REV:	
342	20-08-2026			7	
DRAWN BY:	CHECKED BY:	1 : 2	CDC.02B		
AS	RH				
DRAFTED BY:	CLIENT NAME:				
AS	Umesh Bhandari and Meena Khattri Bhandari				

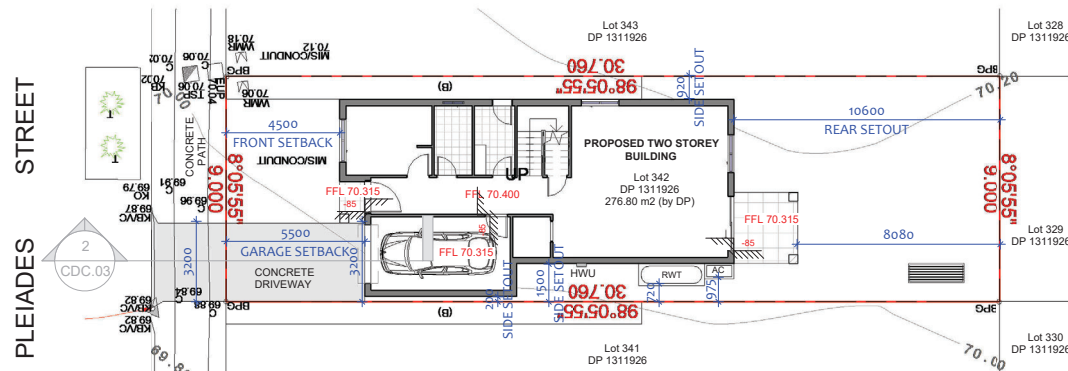

1 CDC - SITE PLAN
1 : 200

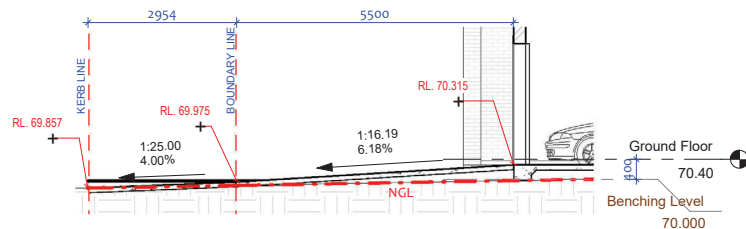

2 DRIVEWAY SECTION
1 : 100

Area Schedule (Bench Plan)	
Sydney Wide Certificate Pty Ltd	
Complying Development Certificate	
Reference: SWC262604/01	
Ground Floor	
Date: 21/08/2026	
CEA	59005035
ALFRESCO	7 m ²

GARAGE	17 m ²
PORCH	2 m ²
Ground Floor: 4	104 m ²
Level 1	
FFA	72 m ²
STAIR VOID	6 m ²
Level 1: 2	78 m ²
Grand total: 6	182 m ²

GREENFIELD HOUSING CODE COMPLIANCE TABLE

DESCRIPTION		COMPLIANCE		COMMENT
ELEMENT	CODE CONTROL	REQUIREMNT	PROPOSED	
LOAND ZONE	1 GENERAL RESIDENTIAL			
LOT NO	LOT 342			
LOT AREA	276.80 m2			
LOT WIDTH	Standard Lot Min. 6m at Building Line facing primary road	6.0m	9 m	YES
HEIGHT	MAX. Height	8.5m	7.6m (MAX.)	YES
FRONT SETBACK	FRONT SET BACK (Min. Setback from Primary Road) For 300-350 sqm. Lot	4.5 m	4.5m	YES
REAR SETBACK (MIN.)	GROUND FLOOR	3m	10.6m	YES
	FIRST FLOOR	6m	10.6 m	
SIDE SETBACK (MIN.)	GROUND FLOOR	0.9/0.9m	0.2/0.92m	NO
	FIRST FLOOR	1.2/0.9m	1.5/0.92m	YES
FLOOR SPACE RATIO (FSR)	75% of lot area	207.60m2	151 m2	YES
GROSS FLOOR AREA PLAN	GROUND FLOOR		79 m2	
	FIRST FLOOR		72 m2	
TOTAL FLOOR AREA			151.0 m2	
ROOF AREA			155 m2	
GARAGE			17m2	
PRIVATE OPEN SPACE	6-10m	16m2	20 m2	YES
LANDSCAPE AREA	10 % of TOTAL LAND AREA	27.68 m2	114 m2	YES

REV	DATE	DESCRIPTION	BY
7	25-06-2026	230 Brick wall in Garage	
1	13-02-2026	Concept Issue	

RUBY HOMES

THIS DRAWING IS THE EXCLUSIVE PROPERTY OF THE DEVELOPER & THE REPRODUCTION OF ANY PART WITHOUT THE PRIOR WRITTEN CONSENT OF THE DEVELOPER IS A VIOLATION OF APPLICABLE LAWS. IN NO EVENT SHALL THE DEVELOPER BE HELD LIABLE FOR SPECIAL COLLATERAL, INCIDENTAL OR CONSEQUENTIAL LIABILITY IN CONNECTION WITH THE USE OF THIS DIGITAL DATA ONCE RELEASED FROM THE DEVELOPERS OFFICE. THIS DRAWING IS TO BE READ & UNDERSTOOD IN CONJUNCTION WITH THE STRUCTURAL, MECHANICAL, ELECTRICAL &/OR ANY OTHER CONSULTANTS' DOCUMENTATION AS MAY BE APPLICABLE TO THE PROJECT PRIOR TO THE START OF ANY WORKS AND FOR ITS DURATION.


PROJECT:
Lot 342 36 PLEIADES STREET
36 PLEIADES STREET
AUSTRAL

DRAWING TITLE:
LOCATION PLAN AND SITE PLAN



LOT NO:	DATE:	SCALE:	DRAWING No:	REV:
342	20-08-2026	As indicated	CDC.03	7
DRAWN BY:	CHECKED BY:			ISSUED BY:
AS	RH			
DRAFTED BY:	CLIENT NAME:			
ID	Umesh Bhandari and Meena Khattri Bhandari			

STREET
PLEIADES

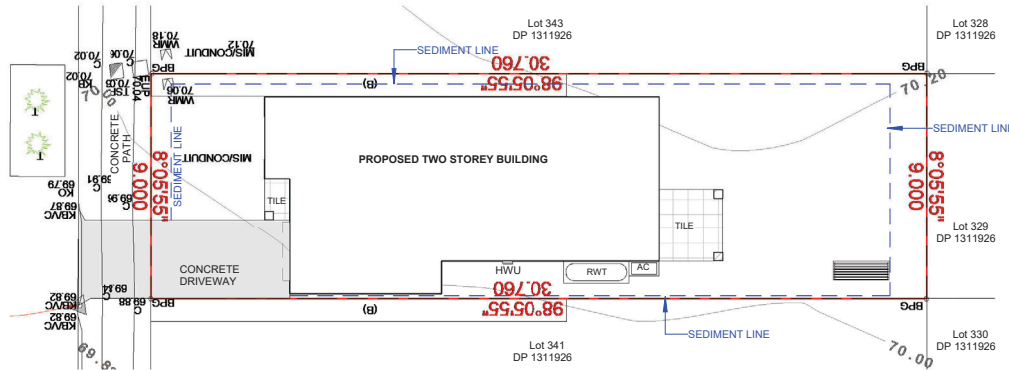

CDC - SITE ANALYSIS AND SEDIMENT CONTROL

1 : 200

TEMPORARY 1.8M HIGH WIRE MESH FENCE WITH DUSTPROOF MESH APPLIED TO FULL HEIGHT TO BOUNDARIES AS REQUIRED

LOCATION OF WASTE BINS
SEDIMENT FENCE AS REQUIRED
GRAVEL ACCESS

SITE ACCESS AREA TO BE USED FOR WASHDOWN AREA

FOOTPATH CLEAN AND CLEAR AT ALL TIMES

LOCATION OF STOCKPILE MATERIAL
MATERIAL STORAGE AREA
TEMPORARY TOILETS
INSTALL TEMPORARY SEDIMENT BARRIERS TO ALL INLET PITS LIKELY TO COLLECT SILT LADEN WATER, TO COUNCIL'S REQUIREMENTS.

SD 6-9 GEOTEXTILE INLET FILTER





- 1) FABRICATE A SEDIMENT BARRIER MADE FROM GEOTEXTILE. REFER SD6-7 FOR DETAILS.
- 2) SUPPORT GEOTEXTILE WITH MESH TIED TO POSTS AT 1 m Ctrs.
- 3) DO NOT COVER INLET WITH GEOTEXTILE

SITE WORKS NOTES

1. ORIGIN OF LEVELS PROVIDED BY SURVEYOR
2. THE BUILDER SHALL VERIFY ALL DIMENSIONS AND EXISTING LEVELS ON SITE PRIOR TO THE COMMENCEMENT OF WORK AND ANY DISCREPANCIES SHALL BE REPORTED TO THE SURVEYOR / ENGINEER.
3. TOPSOIL SHALL BE STRIPPED FROM THE CONSTRUCTION AREA AND STOCKPILED ON SITE, TO BE LATER SPREAD OR DISPOSED OFF SITE, AS DIRECTED BY SUPERVISOR / ENGINEER.
4. ALL TRENCH BACKFILL MATERIAL SHALL BE COMPACTED TO THE SAME DENSITY AS THE ADJACENT MATERIAL.
5. ALL SERVICE TRENCHES UNDER VEHICULAR PAVEMENTS SHALL BE BACKFILLED WITH SAND OR APPROVED GRANULAR MATERIALS, TO THE UNDERSIDE OF THE PAVEMENT, AND COMPACTED TO 98% STANDARD MAXIMUM DRY DENSITY, IN ACCORDANCE WITH AS 1289E1.1.

SD 5-7 STABILISED SITE ACCESS

- 1) STRIP TOPSOIL AND LEVEL SITE.
- 2) COMPACT SUBGRADE.
- 3) COVER AREA WITH GEOTEXTILE.
- 4) CONSTRUCT 200 mm THICK PAD OVER GEOTEXTILE USING ROADBASE OR 30 mm AGGREGATE. Min 15 m LONG OR TO BUILDING ALIGNMENT. Min 3 m WIDE.
- 5) CONSTRUCT HUMP IMMEDIATELY WITHIN BOUNDARY TO DIVERT WATER TO A SEDIMENT FENCE OR OTHER SEDIMENT TRAP.

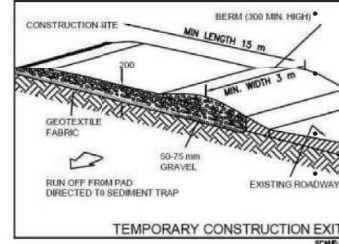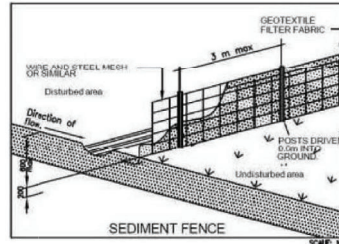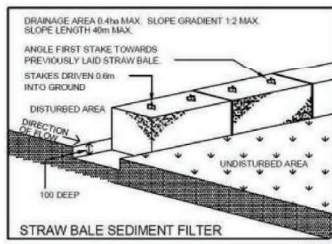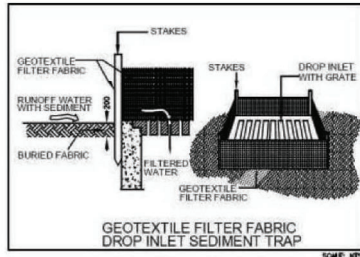

SEDIMENT AND EROSION NOTES:

- THIS PLAN TO BE READ IN CONJUNCTION WITH SEDIMENT AND EROSION CONTROL DETAILS AS ATTACHED.
- THE CONTRACTOR SHALL IMPLEMENT ALL SOIL EROSION AND SEDIMENT CONTROL MEASURES AS NECESSARY AND TO THE SATISFACTION OF COUNCIL PRIOR TO THE COMMENCEMENT OF WORK.
- DISTURBANCE TO THE SITE SHALL BE PERMITTED OTHER THAN IN THE IMMEDIATE AREA OF THE WORK AND NO MATERIAL SHALL BE PLACED OUTSIDE THE LIMIT OF WORKS.
- COUNCIL'S APPROVAL ALL SEDIMENT AND EROSION CONTROL DEVICES TO BE MAINTAINED IN ACCORDANCE WITH STANDARDS OUTLINED IN NSW DEPARTMENT OF HOUSING, MANAGING URBAN STORMWATER-SOILS AND CONSTRUCTIONS".
- TOPSOIL SHALL BE STRIPPED AND STOCKPILED OUTSIDE HAZARD AREAS SUCH AS DRAINAGE LINES. THIS TOP SOIL IS TO BE RESPIRED LATER ON AREAS TO BE REVEGETATED AND STABILISED ONLY. (I.E ALL FOOTPATHS, BATTERS, SITE REGARDING AREAS, BASINS AND CATCH DRAINS). TOPSOIL SHALL NOT BE RESPIRED ON ANY OTHER AREAS UNLESS SPECIALLY INSTRUCTED BY THE SUPERIDENT. IF THEY ARE TO REMAIN FOR LONGER THAN ONE MONTH STOCKPILES SHALL BE PROTECTED FROM EROSION BY COVERING THEM WITH A MULCH AND HYDROSEEDING AND, IF NECESSARY, BY LOCATING BANKS OR DRAINS DOWNSTREAM OF A STOCKPILE TO RETARD SILT LADEN RUNOFF.
- THE CONTRACTOR SHALL REGULARLY MAINTAIN ALL SEDIMENT AND EROSION CONTROL DEVICES AND REMOVE ACCUMULATED SILT FROM SUCH DEVICES SUCH THAT MORE THAN 60% OF THEIR CAPACITY LOST. ALL THE SILTS TO BE PLACED OUTSIDE THE LIMIT OF WORKS. THE PERIOD FOR MAINTAINING THESE DEVICES SHALL BE AT LEAST UNTIL ALL DISTURBED AREAS ARE REVEGETATED AND FURTHER AS MAY BE DIRECTED BY THE SUPERINTENDENT OR COUNCIL.
- LAY TURF STRIP (MIN 300 mm WIDE) ON 100 mm TOPSOIL WITH 1.0 m LONG RETURNS EVERY 6.0m BEHIND ALL KERB AT THE TOP OF ALL BATTERS AND AROUND STRUCTURES IMMEDIATELY AFTER BACKFILLING OR FORMATION.
- THE CONTRACTOR SHALL GRASS SEED ALL DISTURBED AREAS WITH AN APPROVED MIX AS SS ON AS PRACTICABLE AFTER COMPLETION OF EARTHWORKS AND REGRADING.
- VEHICULAR TRAFFIC SHALL BE CONTROLLED DURING CONSTRUCTION CONFINING ACCESS WHERE POSSIBLE TO NOMINATED STABILISED ACCESS POINTS.
- WHEN ANY DEVICES ARE TO BE HANDED OVER TO COUNCIL, THEY SHALL BE IN CLEAN AND STABLE CONDITION.
- THE CONTRACTOR SHALL IMPLEMENT DUST CONTROL BY REGULAR WETTING DOWN (BUT NOT SATURATING) DISTURBED AREA.
- PROVIDE AND MAINTAIN SILT TRAPS AROUND ALL SURFACE INLET PITS UNTIL CATCHMENT IS REVEGETATED OR PAVED.
- REVEGETATE ALL TRENCHES IMMEDIATELY UPON COMPLETION OF BACKFILLING.
- ALL DRAINAGE PIPE INLETS TO BE CAPPED UNTIL:
A) DOWNPIPES CONNECTED
B) PITS CONSTRUCTED & PROTECTED WITH SILT BARRIER

CDC ISSUE

REV	DATE	DESCRIPTION	BY
7	25-06-2026	230 Brick wall in Garage	
1	13-02-2026	Concept Issue	




PROJECT:
Lot 342 36 PLEIADES STREET
36 PLEIADES STREET
AUSTRAL

DRAWING TITLE:
SITE ANALYSIS AND SEDIMENT CONTROL



LOT NO:	DATE:	SCALE:	DRAWING No:	REV:
342	20-08-2026	As indicated	CDC.04	7
DRAWN BY:	CHECKED BY:	CLIENT NAME:	ISSUED BY:	
AS	RH	Umesh Bhandari and Meena Khatri Bhandari		
DRAFTED BY:	ID			

IMPORTANT NOTES:
ALL DIMENSIONS AND NOTES ON ALL PLANS
MUST BE CHECKED AND VERIFIED BY BUILDERS
AND OWNER PRIOR TO COMMENCEMENT OF ANY
BUILDING WORK.
Sydney Wide Centriars Pty Ltd
WITH CONSTRUCTION COMPANY FOR
Complying Development Certificate
PROVIDED FOR CONSTRUCTION ANY WORK
Reference: SWC262604/01
INDICATED ON PLANS IS NOT TO BE MADE
Date: 21/08/2026
PLANS, SPECIFICATIONS MAY NOT BE MADE
Sandres Markham BDC05035
IS THE RESPONSIBILITY OF THE BUILDER/END
USER TO VERIFY PLANS AND SPECIFICATIONS AS
TO THEIR ACCURACY AND COMPLY CURRENT BCA
AND AUSTRALIAN STANDARDS.
WINDOWS TO COMPLY WITH 3.9.3.5 OF THE BCA.

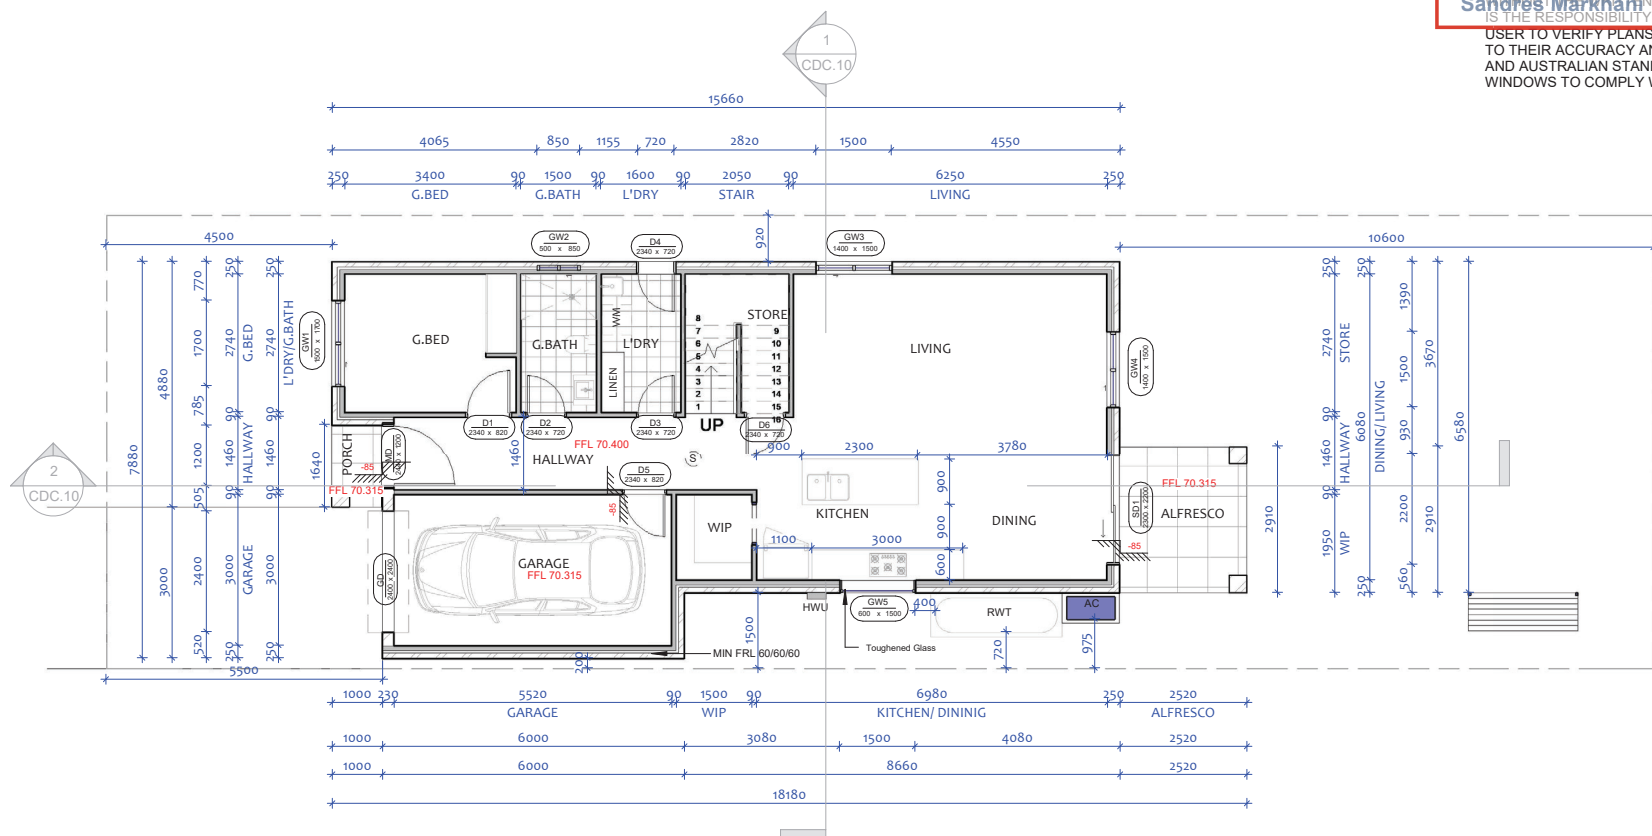

1 Ground Floor
1 : 100

8	20-08-2026	Wardrobe added to G.bed	
7	25-06-2026	230 Brick wall in Garage	
6	30-03-2026	Shower in GF Bath-Ek	
4	23-03-2026	Bathtub added takin space from M.Bed and WIR. Linen Moved to Laundry - Ekta	
3	19-03-2026	Bank Set 1500mm setback as per BEP	
REV	DATE	DESCRIPTION	BY


RUBY HOMES

THIS DRAWING IS THE EXCLUSIVE PROPERTY OF THE DEVELOPER & THE REPRODUCTION OF ANY PART WITHOUT THE PRIOR WRITTEN CONSENT OF THE DEVELOPER IS A VIOLATION OF APPLICABLE LAWS. IN NO EVENT SHALL THE DEVELOPER BE HELD LIABLE FOR SPECIAL, COLLATERAL, INCIDENTAL OR CONSEQUENTIAL LIABILITY IN CONNECTION WITH THE USE OF THIS DIGITAL DATA ONCE RELEASED FROM THE DEVELOPER'S OFFICE. THIS DRAWING IS TO BE READ & UNDERSTOOD IN CONJUNCTION WITH THE STRUCTURAL, MECHANICAL, ELECTRICAL &/ OR ANY OTHER CONSULTANT'S DOCUMENTATION AS MAY BE APPLICABLE TO THE PROJECT PRIOR TO THE START OF ANY WORKS AND FOR ITS DURATION.


PROJECT:
Lot 342 36 PLEIADES STREET
36 PLEIADES STREET
AUSTRAL

DRAWING TITLE:
GROUND FLOOR PLAN

NORTH:


LOT NO:	DATE:	SCALE:	DRAWING No:	REV:
342	20-08-2026	1 : 100	CDC.05	8
DRAWN BY:	CHECKED BY:		ISSUED BY:	
AS	RH			
DRAFTED BY:	CLIENT NAME:			
ID	Umesh Bhandari and Meena Khattri Bhandari			

IMPORTANT NOTES:
ALL DIMENSIONS AND NOTES ON ALL PLANS MUST BE CHECKED AND VERIFIED BY BUILDERS AND OWNER PRIOR TO COMMENCEMENT OF ANY BUILDING WORKS. TO CLARIFY AND CONFIRM WITH CONSTRUCTION COMPANY FOR DISCREPANCIES.
Sydney Wide Certifiers Pty Ltd
Complying Development Certificate
Reference: SWC262604/01
Date: 21/08/2026
Sandesh Markhandi EDC05035
AND AUSTRALIAN STANDARDS:
WINDOWS TO COMPLY WITH 3.9.3.5 OF THE BCA.

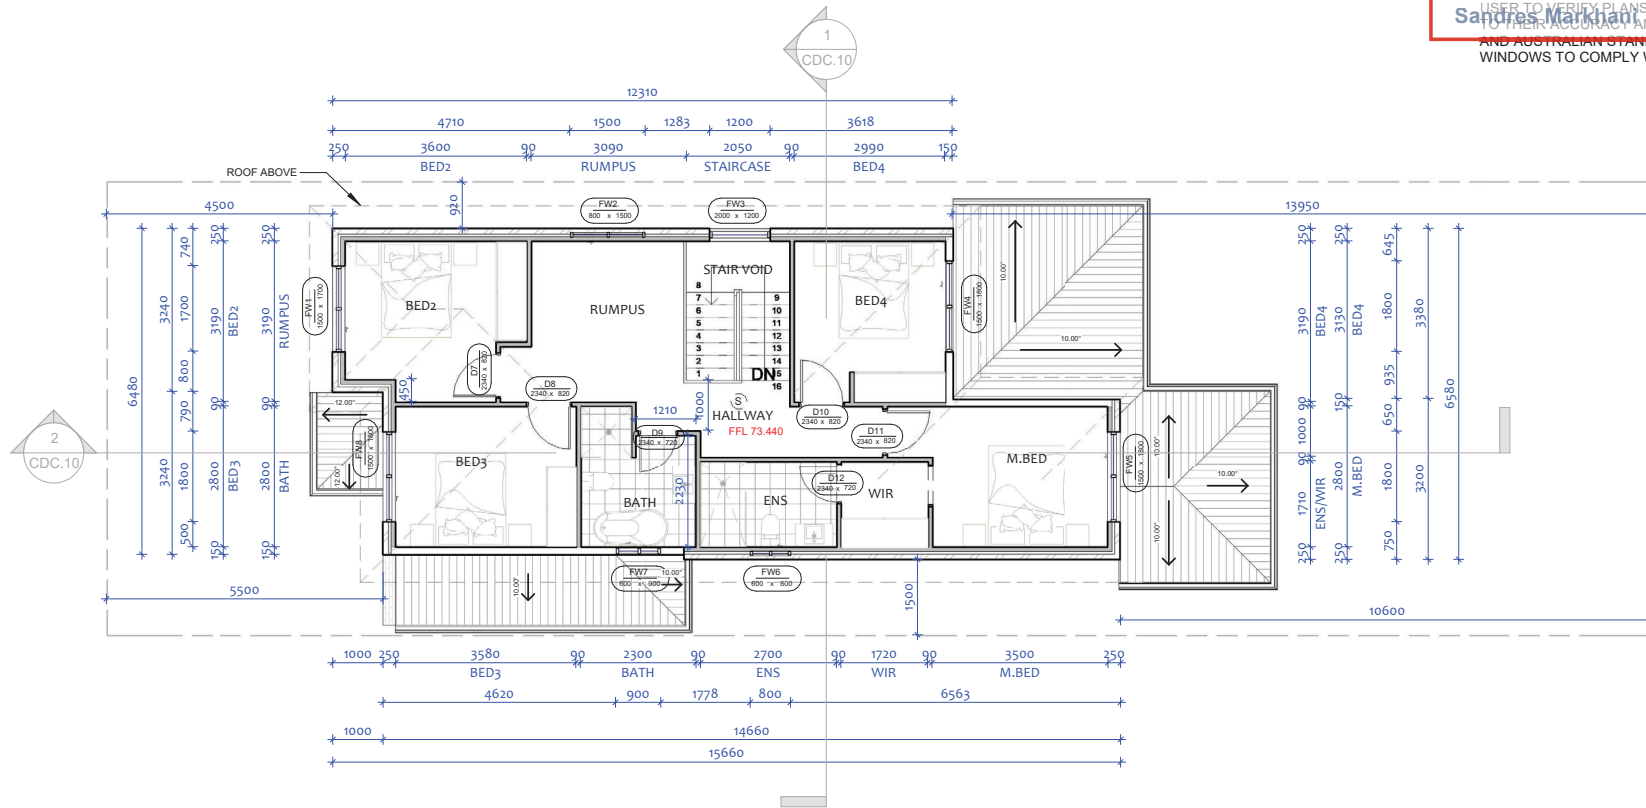

1 Level 1
1 : 100


7	25-06-2026	230 Brick wall in Garage	
5	24-03-2026	Bed2 made 3600, Robe position changed, Store under stairs-Ekta	
4	23-03-2026	Bathlud added takin space from M.Bed and WIR. Linen Moved to Laundry - Ekta	
3	19-03-2026	Bank Set 1500mm setback as per BEP	
2	12-03-2026	Dining relocated to Alfresco space and Alfresco extended outside - Ekta	
REV	DATE	DESCRIPTION	BY

RUBY HOMES

THIS DRAWING IS THE EXCLUSIVE PROPERTY OF THE DEVELOPER & THE REPRODUCTION OF ANY PART WITHOUT THE PRIOR WRITTEN CONSENT OF THE DEVELOPER IS A VIOLATION OF APPLICABLE LAWS. IN NO EVENT SHALL THE DEVELOPER BE HELD LIABLE FOR SPECIAL, COLLATERAL, INCIDENTAL OR CONSEQUENTIAL LIABILITY IN CONNECTION WITH THE USE OF THIS DIGITAL DATA ONCE RELEASED FROM THE DEVELOPER'S OFFICE. THIS DRAWING IS TO BE READ & UNDERSTOOD IN CONJUNCTION WITH THE STRUCTURAL, MECHANICAL, ELECTRICAL & / OR ANY OTHER CONSULTANT'S DOCUMENTATION AS MAY BE APPLICABLE TO THE PROJECT PRIOR TO THE START OF ANY WORKS AND FOR ITS DURATION.


PROJECT:
Lot 342 36 PLEIADES STREET
36 PLEIADES STREET
AUSTRAL

DRAWING TITLE:
FIRST FLOOR LEVEL

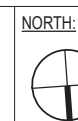

LOT NO:	DATE:	SCALE:	DRAWING No:	REV:
342	20-08-2026	1 : 100	CDC.06	7
DRAWN BY:	CHECKED BY:			ISSUED BY:
AS	RH			
DRAFTED BY:	CLIENT NAME:			
ID	Umesh Bhandari and Meena Khattri Bhandari			

CDC ISSUE

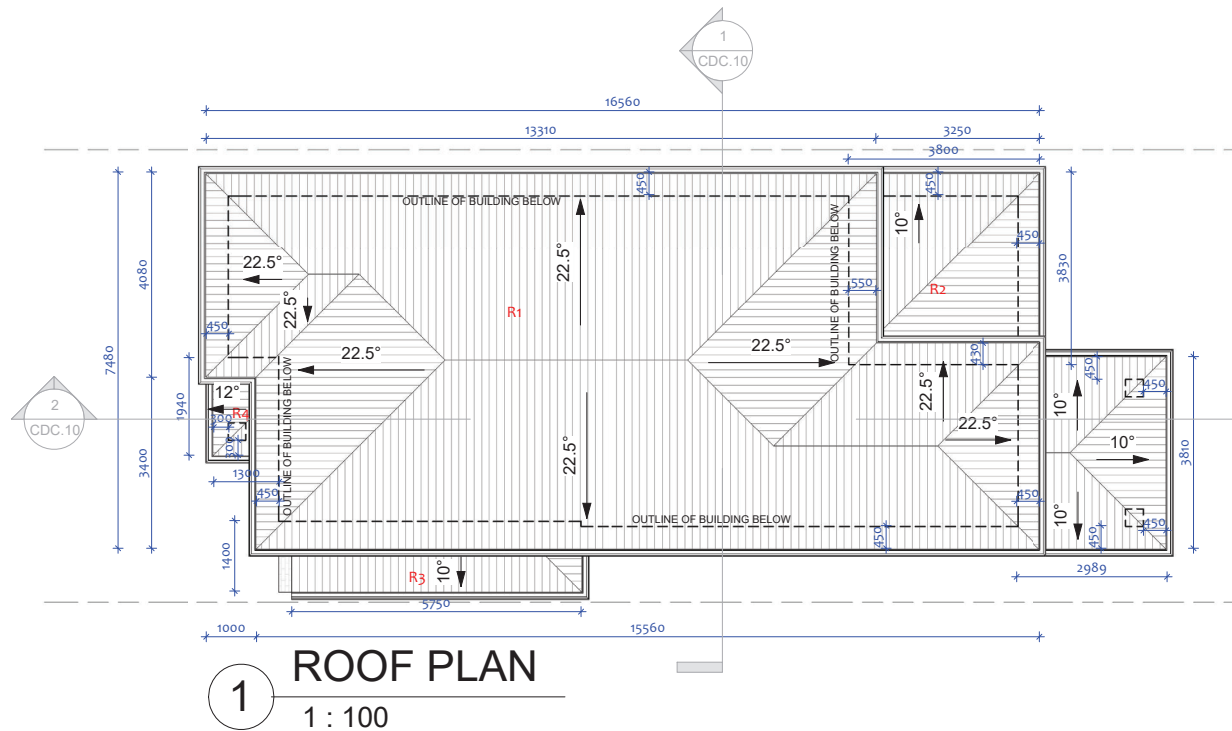

IMPORTANT NOTES:
ALL DIMENSIONS AND NOTES ON ALL PLANS MUST BE CHECKED AND VERIFIED BY BUILDERS AND OWNER PRIOR TO COMMENCEMENT OF ANY BUILDING WORK.
Sydney Wide Certifiers Pty Ltd
Complying Development Certificate
Reference: SWC 262604701
Date: 21/08/2026
Sandree Mariani CDC05035
BUILDING WORKS MUST BE COMPLETED IN ACCORDANCE WITH CONSTRUCTION COMPANY FOR DISCREPANCIES ON ALL DOCUMENTS AND PLANS PROVIDED FOR CONSTRUCTION ANY WORK INDICATED ON THE PLAN BUT NOT IN THE SPECIFICATIONS SHALL BE AT THE DEVELOPER'S PART OF THE CONTRACT VARIATION TO PLANS, SPECIFIC INSTRUCTIONS MADE WITHOUT THE WRITTEN CONSENT OF OWNER IT TO THEIR ACCURACY AND COMPLY CURRENT BCA AND AUSTRALIAN STANDARDS. WINDOWS TO COMPLY WITH 3.9.3.5 OF THE BCA.

Roof Schedule			
Mark	Base Level	Area	Comments
R2	Level 1	26 m ²	COLORBOND
R1	CEILING LEVEL	118 m ²	COLORBOND
R4	Ground Ceiling Level	3 m ²	COLORBOND
R3	Level 1	8 m ²	COLORBOND
Grand total: 4		155 m ²	


REV	DATE	DESCRIPTION	BY
7	25-06-2026	230 Brick wall in Garage	
4	23-03-2026	Bathlup added takin space from M.Bed and WIR. Linen Moved to Laundry - Ekta	
3	19-03-2026	Bank Set 1500mm setback as per BEP	
1	13-02-2026	Concept Issue	

RUBY HOMES



THIS DRAWING IS THE EXCLUSIVE PROPERTY OF THE DEVELOPER & THE REPRODUCTION OF ANY PART WITHOUT THE PRIOR WRITTEN CONSENT OF THE DEVELOPER IS A VIOLATION OF APPLICABLE LAWS. IN NO EVENT SHALL THE DEVELOPER BE HELD LIABLE FOR SPECIAL COLLATERAL, INCIDENTAL OR CONSEQUENTIAL LIABILITY IN CONNECTION WITH THE USE OF THIS DIGITAL DATA ONCE RELEASED FROM THE DEVELOPER'S OFFICE. THIS DRAWING IS TO BE READ & UNDERSTOOD IN CONJUNCTION WITH THE STRUCTURAL, MECHANICAL, ELECTRICAL & / OR ANY OTHER CONSULTANTS' DOCUMENTATION AS MAY BE APPLICABLE TO THE PROJECT PRIOR TO THE START OF ANY WORKS AND FOR ITS DURATION.

PROJECT:
Lot 342 36 PLEIADES STREET
36 PLEIADES STREET
AUSTRAL

DRAWING TITLE:
ROOF PLAN

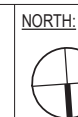

LOT NO:	DATE:	SCALE:	DRAWING No:	REV:
342	20-08-2026	1 : 100	CDC.07	7
DRAWN BY:	CHECKED BY:			ISSUED BY:
AS	RH			
DRAFTED BY:	CLIENT NAME:			
ID	Umesh Bhandari and Meena Khattri Bhandari			

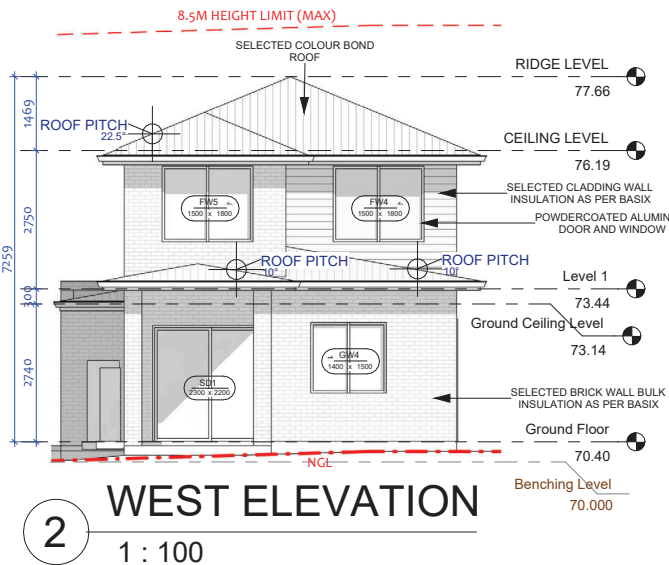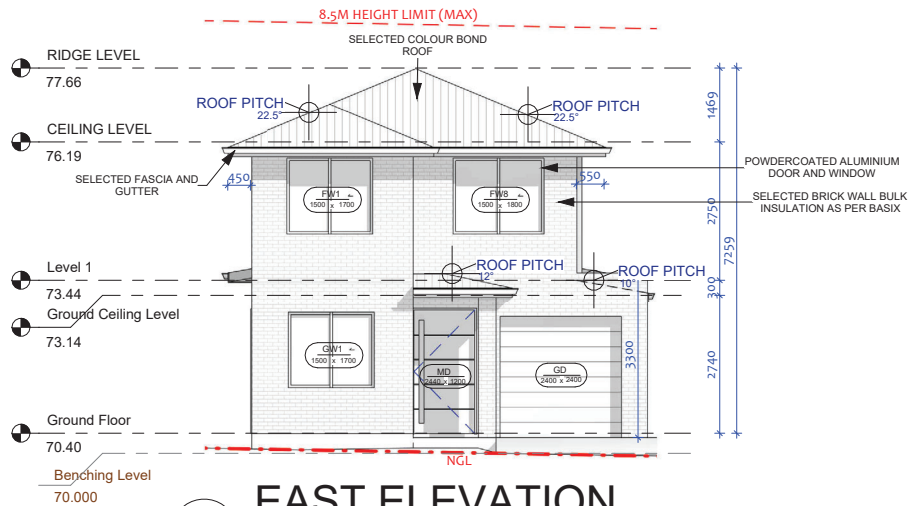

Window Schedule 1					
Mark	Height	Width	Sill Height	Head Height	Description
Ground Floor					
GW1	1500	1700	900	2400	SLIDING
GW2	500	850	1900	2400	SLIDING
GW3	1400	1500	1000	2400	SLIDING
GW4	1400	1500	1000	2400	SLIDING
GW5	600	1500	1050	1650	FIXED

Ground Floor: 5

Level 1					
FW1	1500	1700	950	2450	SLIDING
FW2	800	1500	1650	2450	SLIDING
FW3	2000	1200	450	2450	FIXED
FW4	1500	1800	950	2450	SLIDING
FW5	1500	1800	950	2450	SLIDING
FW6	600	800	1850	2450	SLIDING
FW7	600	900	1850	2450	SLIDING
FW8	1500	1800	950	2450	SLIDING

Level 1: 8

Door Schedule 1				
Mark	Height	Width	Count	Description
Ground Floor				
D1	2340	820	1	FLUSH DOOR
D2	2340	720	1	FLUSH DOOR
D3	2340	720	1	FLUSH DOOR
D4	2340	720	1	FLUSH DOOR
D5	2340	820	1	FLUSH DOOR
D6	2340	720	1	FLUSH DOOR
GD	2400	2400	1	GARAGE DOOR
MD	2440	1200	1	SOLID CORE DOOR
SD1	2300	2200	1	SLIDING DOOR

Ground Floor: 9

Level 1				
D7	2340	820	1	FLUSH DOOR
D8	2340	820	1	FLUSH DOOR
D9	2340	720	1	FLUSH DOOR
D10	2340	820	1	FLUSH DOOR
D11	2340	820	1	FLUSH DOOR
D12	2340	720	1	FLUSH DOOR

Level 1: 6

REV	DATE	DESCRIPTION	BY
7	25-06-2026	230 Brick wall in Garage	
4	23-03-2026	Bathlud added takin space from M.Bed and WIR. Linen Moved to Laundry - Ekta	
3	19-03-2026	Bank Setl 1500mm setback as per BEP	
1	13-02-2026	Concept Issue	

RUBY HOMES

THIS DRAWING IS THE EXCLUSIVE PROPERTY OF THE DEVELOPER & THE REPRODUCTION OF ANY PART WITHOUT THE PRIOR WRITTEN CONSENT OF THE DEVELOPER IS A VIOLATION OF APPLICABLE LAWS. IN NO EVENT SHALL THE DEVELOPER BE HELD LIABLE FOR SPECIAL, COLLATERAL, INCIDENTAL OR CONSEQUENTIAL LIABILITY IN CONNECTION WITH THE USE OF THIS DIGITAL DATA ONCE RELEASED FROM THE DEVELOPER'S OFFICE. THIS DRAWING IS TO BE READ & UNDERSTOOD IN CONJUNCTION WITH THE STRUCTURAL, MECHANICAL, ELECTRICAL & / OR ANY OTHER CONSULTANT'S DOCUMENTATION AS MAY BE APPLICABLE TO THE PROJECT PRIOR TO THE START OF ANY WORKS AND FOR ITS DURATION.


PROJECT:
Lot 342 36 PLEIADES STREET
36 PLEIADES STREET
AUSTRAL

DRAWING TITLE:
ELEVATION 01


NORTH:

LOT NO:	DATE:	SCALE:	DRAWING No:	REV:
342	20-08-2026	1 : 100	CDC.08	7
DRAWN BY:	CHECKED BY:			ISSUED BY:
AS	RH			
DRAFTED BY:	CLIENT NAME:			
ID	Umesh Bhandari and Meena Khattri Bhandari			

CDC ISSUE

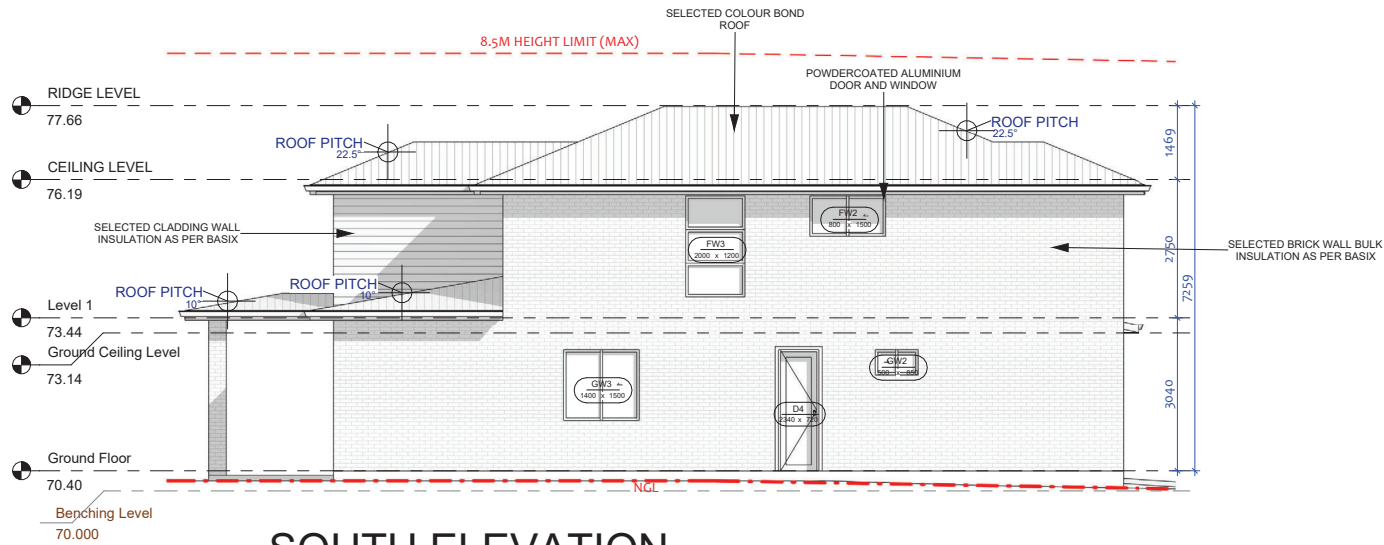

1 SOUTH ELEVATION
1 : 100

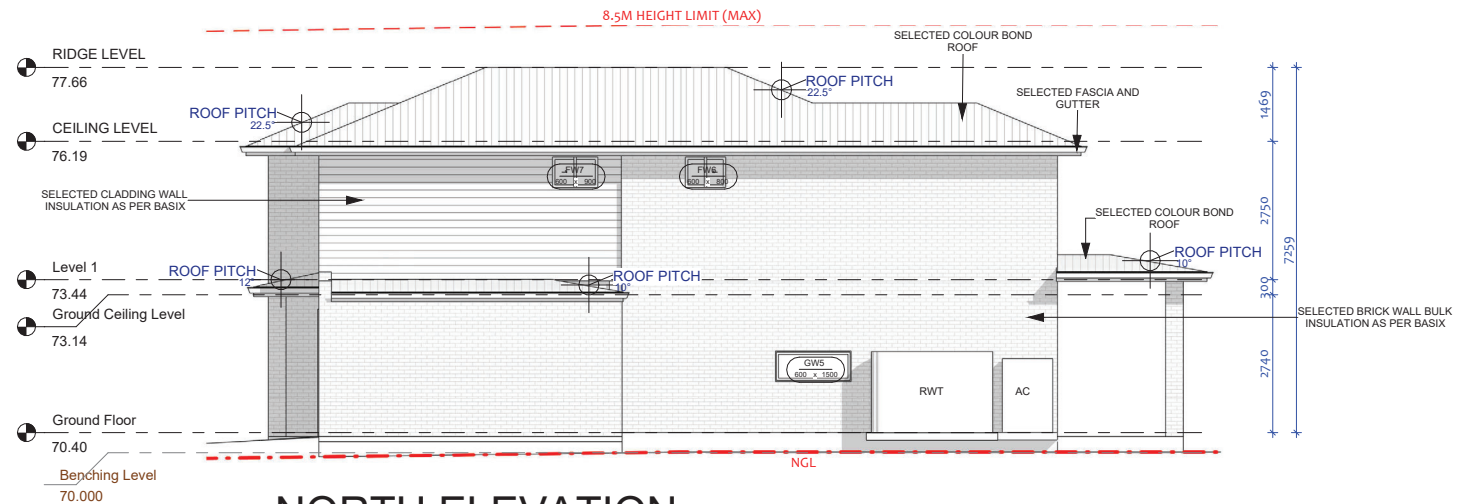

2 NORTH ELEVATION
1 : 100

Sydney Wide Certifiers Pty Ltd
Complying Development Certificate
Reference: SWC262604/01
Date: 21/08/2026
Sandres Markhani BDC05035

REV	DATE	DESCRIPTION	BY
7	25-06-2026	230 Brick wall in Garage	
4	23-03-2026	Bathub added takin space from M.Bed and WIR. Linen Moved to Laundry - Ekta	
3	19-03-2026	Bank Set 1500mm setback as per BEP	
1	13-02-2026	Concept Issue	

RUBY HOMES

THIS DRAWING IS THE EXCLUSIVE PROPERTY OF THE DEVELOPER & THE REPRODUCTION OF ANY PART WITHOUT THE PRIOR WRITTEN CONSENT OF THE DEVELOPER IS A VIOLATION OF APPLICABLE LAWS. IN NO EVENT SHALL THE DEVELOPER BE HELD LIABLE FOR SPECIAL, COLLATERAL, INCIDENTAL OR CONSEQUENTIAL LIABILITY IN CONNECTION WITH THE USE OF THIS DIGITAL DATA ONCE RELEASED FROM THE DEVELOPER'S OFFICE. THIS DRAWING IS TO BE READ & UNDERSTOOD IN CONJUNCTION WITH THE STRUCTURAL, MECHANICAL, ELECTRICAL &/OR ANY OTHER CONSULTANT'S DOCUMENTATION AS MAY BE APPLICABLE TO THE PROJECT PRIOR TO THE START OF ANY WORKS AND FOR ITS DURATION.


PROJECT:
Lot 342 36 PLEIADES STREET
36 PLEIADES STREET
AUSTRAL

DRAWING TITLE:
ELEVATION 02

NORTH:


LOT NO:	DATE:	SCALE:	DRAWING No:	REV:
342	20-08-2026	1 : 100	CDC.09	7
DRAWN BY:	CHECKED BY:			ISSUED BY:
AS	RH			
DRAFTED BY:	CLIENT NAME:			
ID	Umesh Bhandari and Meena Khattri Bhandari			

CDC ISSUE

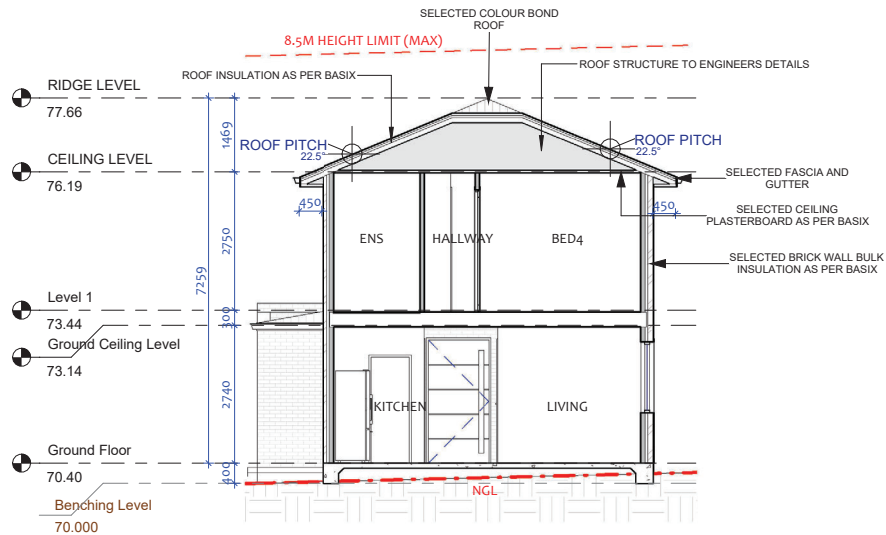

1 CROSS SECTION
1 : 100

Sydney Wide Certifiers Pty Ltd
Complying Development Certificate
Reference: SWC262604/01
Date: 21/08/2026
Sandres Markhani BDC05035

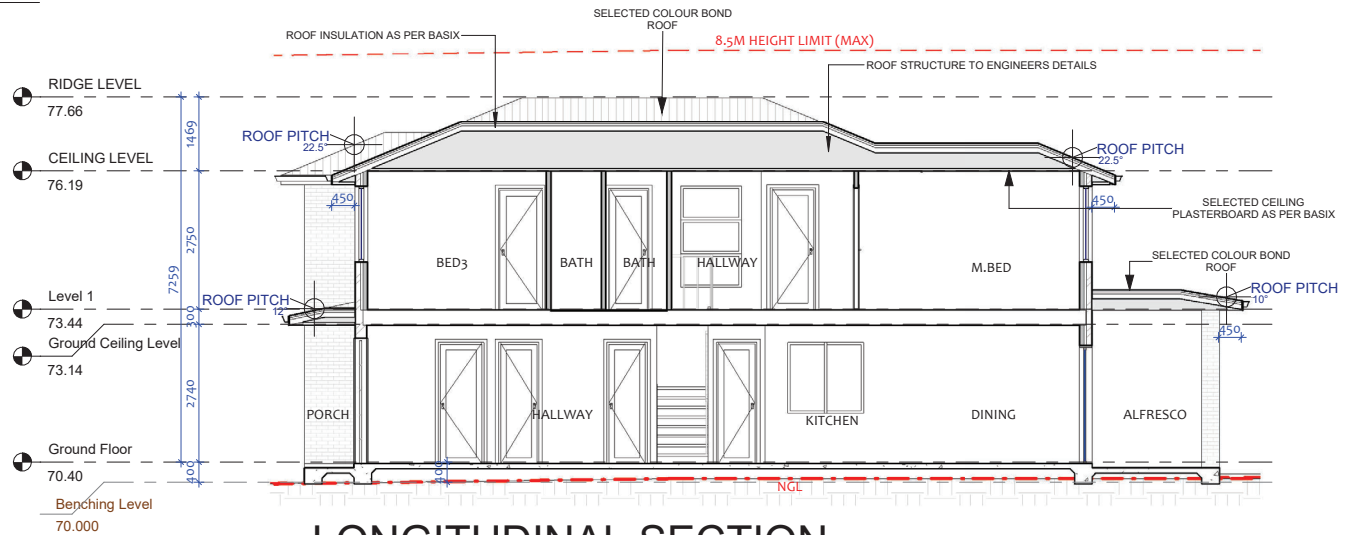

2 LONGITUDINAL SECTION
1 : 100

REV	DATE	DESCRIPTION	BY
7	25-06-2026	230 Brick wall in Garage	
1	13-02-2026	Concept Issue	

RUBY HOMES

THIS DRAWING IS THE EXCLUSIVE PROPERTY OF THE DEVELOPER & THE REPRODUCTION OF ANY PART WITHOUT THE PRIOR WRITTEN CONSENT OF THE DEVELOPER IS A VIOLATION OF APPLICABLE LAWS. IN NO EVENT SHALL THE DEVELOPER BE HELD LIABLE FOR SPECIAL, COLLATERAL, INCIDENTAL OR CONSEQUENTIAL LIABILITY IN CONNECTION WITH THE USE OF THIS DIGITAL DATA ONCE RELEASED FROM THE DEVELOPER'S OFFICE. THIS DRAWING IS TO BE READ & UNDERSTOOD IN CONJUNCTION WITH THE STRUCTURAL, MECHANICAL, ELECTRICAL & / OR ANY OTHER CONSULTANT DOCUMENTATION AS MAY BE APPLICABLE TO THE PROJECT PRIOR TO THE START OF ANY WORKS AND FOR ITS DURATION.


PROJECT:
**Lot 342 36 PLEIADES STREET
36 PLEIADES STREET
AUSTRAL**

DRAWING TITLE:
SECTIONS

NORTH:

LOT NO:	DATE:	SCALE:	DRAWING No:	REV:
342	20-08-2026	1 : 100	CDC.10	7
DRAWN BY:	CHECKED BY:			ISSUED BY:
AS	RH			
DRAFTED BY:	CLIENT NAME:			
ID	Umesh Bhandari and Meena Khattri Bhandari			

CDC ISSUE

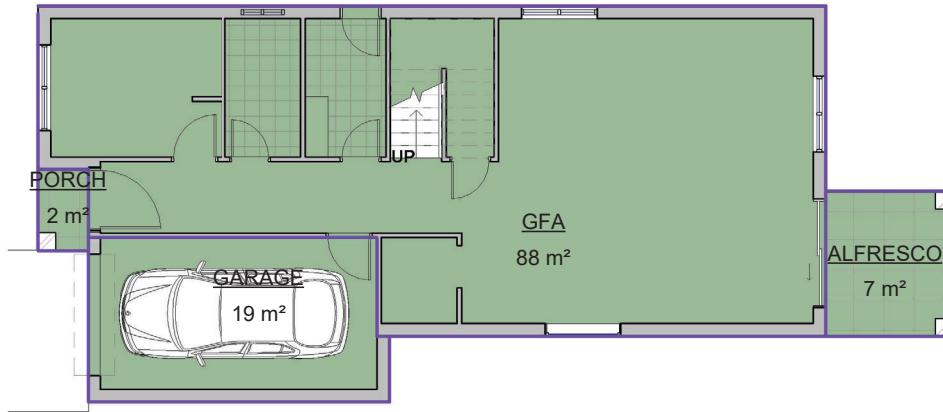

1 Ground Floor
1 : 100

Area Schedule (Gross Building)	
Name	Area

Ground Floor	
GFA	88 m²
ALFRESCO	7 m²
GARAGE	19 m²
PORCH	2 m²


Ground Floor: 4 116 m²

Level 1	
FFA	84 m²
STAIRCASE VOID	6 m²

Level 1: 2 89 m²

Grand total: 6 206 m²

Sydney Wide Certifiers Pty Ltd
Complying Development Certificate
Reference: SWC262604/01
Date: 21/08/2026
Sandres Markhani BDC05035

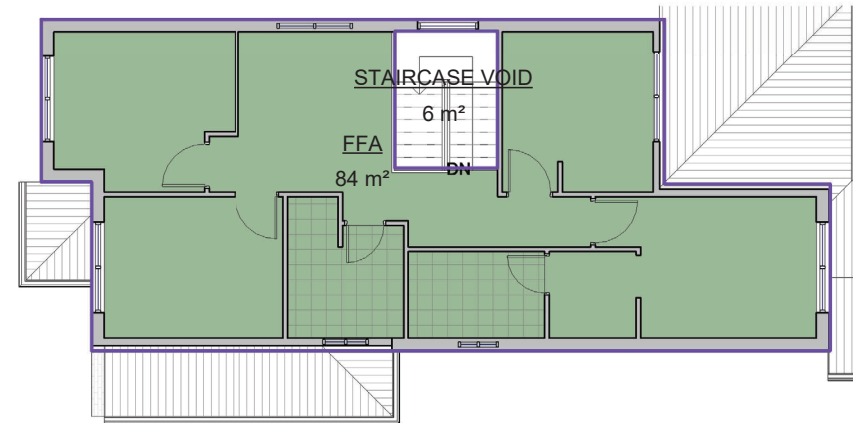

2 Level 1
1 : 100

REV	DATE	DESCRIPTION	BY
7	25-06-2026	230 Brick wall in Garage	
4	23-03-2026	Bathlud added takin space from M.Bed and WIR. Linen Moved to Laundry - Ekta	
3	19-03-2026	Bank Setl 1500mm setback as per BEP	
1	13-02-2026	Concept Issue	

RUBY HOMES

THIS DRAWING IS THE EXCLUSIVE PROPERTY OF THE DEVELOPER & THE REPRODUCTION OF ANY PART WITHOUT THE PRIOR WRITTEN CONSENT OF THE DEVELOPER IS A VIOLATION OF APPLICABLE LAWS. IN NO EVENT SHALL THE DEVELOPER BE HELD LIABLE FOR SPECIAL, COLLATERAL, INCIDENTAL OR CONSEQUENTIAL LIABILITY IN CONNECTION WITH THE USE OF THIS DIGITAL DATA ONCE RELEASED FROM THE DEVELOPERS OFFICE. THIS DRAWING IS TO BE READ & UNDERSTOOD IN CONJUNCTION WITH THE STRUCTURAL, MECHANICAL, ELECTRICAL & / OR ANY OTHER CONSULTANTS DOCUMENTATION AS MAY BE APPLICABLE TO THE PROJECT PRIOR TO THE START OF ANY WORKS AND FOR ITS DURATION.


PROJECT:
Lot 342 36 PLEIADES STREET
36 PLEIADES STREET
AUSTRAL

DRAWING TITLE:
FLOOR AREA PLAN




LOT NO:	DATE:	SCALE:	DRAWING No.	REV:
342	20-08-2026	1 : 100	CDC.11	7
DRAWN BY:	CHECKED BY:			ISSUED BY:
AS	RH			
DRAFTED BY:	CLIENT NAME:			
ID	Umesh Bhandari and Meena Khattri Bhandari			

CDC ISSUE

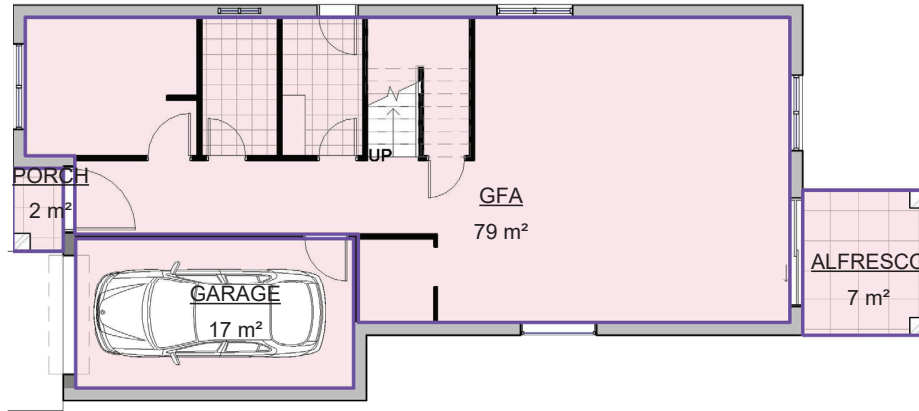

1 Ground Floor
1 : 100

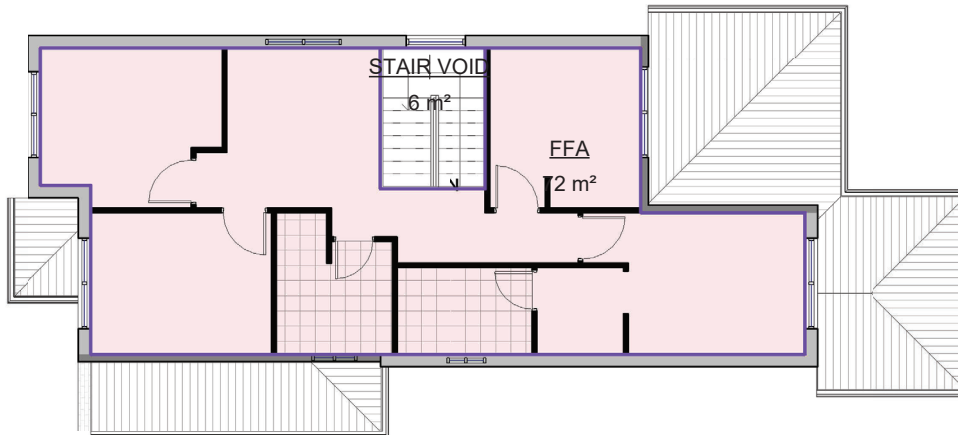

2 Level 1
1 : 100

Sydney Wide Certifiers Pty Ltd
Complying Development Certificate

Reference: SWC262604/01

Date: 21/08/2026

Sandres Markhani BDC05035

Area Schedule (Rentable)

Name	Area
------	------

Ground Floor

GFA	79 m²
ALFRESCO	7 m²
GARAGE	17 m²
PORCH	2 m²

Ground Floor: 4 104 m²

Level 1

FFA	72 m²
STAIR VOID	6 m²

Level 1: 2 78 m²

Grand total: 6 182 m²

REV	DATE	DESCRIPTION	BY
7	25-06-2026	230 Brick wall in Garage	
1	13-02-2026	Concept Issue	

RUBY HOMES

THIS DRAWING IS THE EXCLUSIVE PROPERTY OF THE DEVELOPER & THE REPRODUCTION OF ANY PART WITHOUT THE PRIOR WRITTEN CONSENT OF THE DEVELOPER IS A VIOLATION OF APPLICABLE LAWS. IN NO EVENT SHALL THE DEVELOPER BE HELD LIABLE FOR SPECIAL, COLLATERAL, INCIDENTAL OR CONSEQUENTIAL LIABILITY IN CONNECTION WITH THE USE OF THIS DIGITAL DATA ONCE RELEASED FROM THE DEVELOPER'S OFFICE. THIS DRAWING IS TO BE READ & UNDERSTOOD IN CONJUNCTION WITH THE STRUCTURAL, MECHANICAL, ELECTRICAL & / OR ANY OTHER CONSULTANT'S DOCUMENTATION AS MAY BE APPLICABLE TO THE PROJECT PRIOR TO THE START OF ANY WORKS AND FOR ITS DURATION.

PROJECT:
Lot 342 36 PLEIADES STREET
36 PLEIADES STREET
AUSTRAL

DRAWING TITLE:
RENTABLE AREA PLAN



LOT NO:	DATE:	SCALE:	DRAWING No:	REV:
342	20-08-2026	1 : 100	CDC.12	7
DRAWN BY:	CHECKED BY:			
AS	RH			
DRAFTED BY:	CLIENT NAME:			
ID	Umesh Bhandari and Meena Khattri Bhandari			

CDC ISSUE

Sydney Wide Certifiers Pty Ltd
Complying Development Certificate
Reference: SWC262604/01
Date: 21/08/2026
Sandres Markhani BDC05035



	1. RF	2. BR1	3. CD1	4. AL	5. ED	6. GD	7. FAS	8. GUT
	ROOF	MAIN WALLS	CLADDING	WINDOWS/ BALUSTRADE	MAIN DOOR	GARAGE DOOR	FASCIA	GUTTER
MATERIAL	COLORBOND	BRICK	BLUEBOARD	ALUMINIUM	TIMBER	COLORBOND	COLORBOND	COLORBOND
COLOR								

NOTE: ALL COLOURS SPECIFIED ARE INDICATIVE ONLY AND ARE SUBJECT TO VARIATION AND TO AVAILABILITY
ANY DISCREPANCY PLEASE FOLLOW AS PER RENDERED IMAGE

REV	DATE	DESCRIPTION	BY
7	25-06-2026	230 Brick wall in Garage	
1	13-02-2026	Concept Issue	

RUBY
HOMES

THIS DRAWING IS THE EXCLUSIVE PROPERTY OF THE DEVELOPER & THE REPRODUCTION OF ANY PART WITHOUT THE PRIOR WRITTEN CONSENT OF THE DEVELOPER IS A VIOLATION OF APPLICABLE LAWS. IN NO EVENT SHALL THE DEVELOPER BE HELD LIABLE FOR SPECIAL COLLATERAL, INCIDENTAL OR CONSEQUENTIAL LIABILITY IN CONNECTION WITH THE USE OF THIS DIGITAL DATA ONCE RELEASED FROM THE DEVELOPER'S OFFICE. THIS DRAWING IS TO BE READ & UNDERSTOOD IN CONJUNCTION WITH THE STRUCTURAL, MECHANICAL, ELECTRICAL &/OR ANY OTHER CONSULTANTS' DOCUMENTATION AS MAY BE APPLICABLE TO THE PROJECT PRIOR TO THE START OF ANY WORKS AND FOR ITS DURATION.


PROJECT:
Lot 342 36 PLEIADES STREET
36 PLEIADES STREET
AUSTRAL

DRAWING TITLE:
COLOR SCHEDULE

NORTH:

LOT NO:	DATE:	SCALE:	DRAWING No:	REV:
342	20-08-2026	1 : 100	CDC.14	7
DRAWN BY:	CHECKED BY:			ISSUED BY:
AS	RH			
DRAFTED BY:	CLIENT NAME:			
ID	Umesh Bhandari and Meena Khattri Bhandari			

Sydney Wide Certifiers Pty Ltd
Complying Development Certificate
Reference: SWC262604/01
Date: 21/08/2026
Sandres Markhani BDC05035

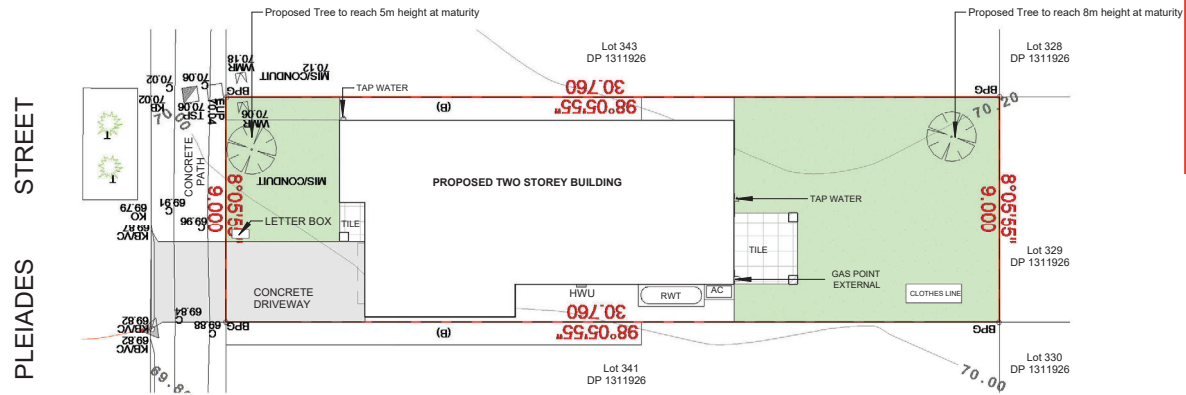

1

CDC -LANDSCAPE PLAN
1 : 200

LANDSCAPE AREA	
FRONT AREA	26 m ²
BACKYARD AREA	88 m ²

GENERAL NOTES:

- LANDSCAPE CONTRACTOR TO CHECK DA CONDITIONS AND STAMPED LANDSCAPE PLAN BEFORE COMMENCING WORKS TO ENSURE NO ADDITIONS/AMENDMENTS TO PLAN.
- GARDEN BEDS IN OSD BASIN TO CONSIST OF NON FLOATABLE DECORATIVE GRAVEL.
- REFER TO HYDRAULICS ENGINEERS PLAN FOR OSD DETAILS/FINAL LEVELS.
- MULCHED PLANTING BEDS TO BE A MINIMUM DEPTH OF 75mm AS SELECTED.
- CONTRACTOR'S RESPONSIBILITY TO CHECK AND ADJUST SOIL pH AS REQUIRED.
- PROVIDE TIMBER EDGE AS A MINIMUM BENEATH FENCING/GATES TO DEFINE TURF AND GARDEN BEDS/PATHWAYS.EDGING TO BE PROVIDED TO ALL AREAS WHERE DIFFERING MATERIALS MEET i.e TURF/GARDEN,TURF/GRAVEL PATH ETC.
- WEED MAT BENEATH GRAVEL PATHWAYS REQUIRED TO LIMIT MUD TRACKING.
- PREMIUM ORGANIC GARDEN MIX TO BE USED.
- ALL PLANTS TO BE HEALTHY AND VIGOROUS.
- CONTRACTOR TO MAKE GOOD TURF ON NATURE STRIP POST CONSTRUCTION.
- CONTRACTOR TO MAKE GOOD TURF ON NATURE STRIP POST CONSTRUCTION.
- DO NOT SCALE ARCHITECTURAL SETOUT FROM LANDSCAPE DRAWING.
- EXISTING TREE SPREAD APPROXIMATE ONLY.REFER TO TREE REPORT WHEN APPLICABLE.
- SITE SURVEY PROVIDED BY OTHERS.
- BUFFALO TURF PREFERRED OVER KIKUYU.

LANDSCAPE BASIX NOTE:


THE APPLICANT MUST PLANT INDIGENEOUS OR LOW WATER USE SPECIES OF VEGETATION THROUGHOUT 15 SQM OF THE SITE.

NOTE :BUILDER RESERVES THE RIGHT NOT TO UNDERTAKE NOR SUPPLY CERTIFICATE FOR OCCUPATION CERTIFICATE.

NOTE : TO AID COMPLIANCE WITH BASIX LEGISLATION,PLANTS (WHERE APPLICABLE) HAVE BEEN SELECTED FROM THE LOCAL CITY COUNCIL/SHIRE PLANT LISTS.


NOTE: LOCATION OF SEWER MAINS/LINES,WATER PIPES,UNDERGROUND ELECTRICITY AND OTHER SERVICES MUST BE OBTAINED PRIOR TO COMMENCEMENT OF ANY WORK ON SITE.

CONTRACTORS NOTE : CALCULATED AREAS DETERMINED BY CAD AND HAVE BEEN ROUNDED UP FOR USE AS A GUIDE ONLY ALLOW STANDARD PERCENTAGE FOR CUTTING AND WASTAGE .CONFIRM DIMENSIONS AND NUMBERS PRIOR TO QUOTING/ORDERING.

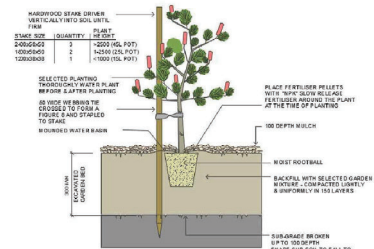

2. TREE & SHRUB PLANTING IN GARDEN BED

NOTE:
DO NOT PLANT IN UNSUITABLE WEATHER CONDITIONS SUCH AS EXTREME HEAT, COLD, WIND OR RAIN.
CLAY SOILS TO BE TREATED WITH CLAY BREAKER AND ORGANIC COMPOST.

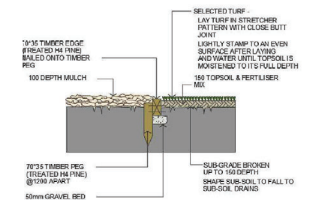

1. TURF & GARDEN EDGE DETAIL

NOTE:
ALIGNMENT OF BRICK EDGE SHALL BE EVEN & FREE FROM DIPS AND HUMPS.

REV	DATE	DESCRIPTION	BY
7	25-06-2026	230 Brick wall in Garage	
1	13-02-2026	Concept Issue	

RUBY HOMES

THIS DRAWING IS THE EXCLUSIVE PROPERTY OF THE DEVELOPER & THE REPRODUCTION OF ANY PART WITHOUT THE PRIOR WRITTEN CONSENT OF THE DEVELOPER IS A VIOLATION OF APPLICABLE LAWS. IN NO EVENT SHALL THE DEVELOPER BE HELD LIABLE FOR SPECIAL, COLLATERAL, INCIDENTAL OR CONSEQUENTIAL LIABILITY IN CONNECTION WITH THE USE OF THIS DIGITAL DATA ONCE RELEASED FROM THE DEVELOPER'S OFFICE. THIS DRAWING IS TO BE READ & UNDERSTOOD IN CONJUNCTION WITH THE STRUCTURAL, MECHANICAL, ELECTRICAL & / OR ANY OTHER CONSULTANT'S DOCUMENTATION AS MAY BE APPLICABLE TO THE PROJECT PRIOR TO THE START OF ANY WORKS AND FOR ITS DURATION.

PROJECT:
Lot 342 36 PLEIADES STREET
36 PLEIADES STREET
AUSTRAL

DRAWING TITLE:
LANDSCAPE PLAN

NORTH:



LOT NO:	DATE:	SCALE:	DRAWING No:	REV:
342	20-08-2026	1 : 200	CDC.15	7
DRAWN BY:	CHECKED BY:			ISSUED BY:
AS	RH			
DRAFTED BY:	CLIENT NAME:			
ID	Umesh Bhandari and Meena Khatri Bhandari			

ABCB HOUSING PROVISIONS : PART 10.2 WET AREA WATERPROOFING

10.2.1 Wet Areas

1. Building elements in wet areas within a building must be protected with a waterproofing system.
2. The waterproofing system in (1) must be either waterproof or water resistant in accordance with 10.2.2 to 10.2.6.

10.2.2 Shower Area (enclosed and unenclosed)

1. For a shower area with a hob, step-down or level threshold, the following applies:
a. The floor of the shower area must be waterproof, including any hob or step-down (see Figure 10.2.2); and
b. The walls of the shower area must be waterproof not less than 1800 mm above the floor substrate (see Figure 10.2.2).
c. Wall junctions and joints within the shower area must be waterproof not less than 40 mm either side of the junction (see Figure 10.2.2).
d. Wall/floor junctions within the shower area must be waterproof (see Figure 10.2.2).
e. Penetrations within the shower area must be waterproof.
2. A shower with a preformed shower base must also comply with the requirements of (1), except for (a) which is not applicable.

Figure 10.2.2: Extent of treatment for shower areas - concrete compressed fibre-cement and fibre-cement sheet floors.

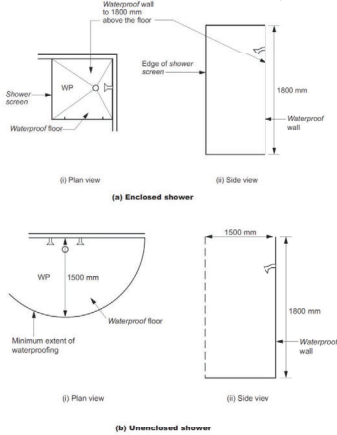


Figure Notes
Wall/floor junction heights are to be as per 10.2.2 to 10.2.6 (as applicable).

Notes
Where a shower is above a bath or spa, use requirements for shower.

10.2.3 Area outside shower area

1. For concrete, compressed fibre-cement and fibre-cement sheet flooring, the floor of the room must be water resistant.
2. For timber floors including particleboard, plywood and other timber based flooring materials, the floor of the room must be waterproof.
3. Wall/floor junctions must be -
a. waterproof, and
b. where a flashing is used, the horizontal leg must be not less than 40 mm.

10.2.4 Areas adjacent to baths and spas without showers

1. For areas adjacent to all baths and spas, the following applies:
a. For concrete, compressed fibre-cement and fibre-cement sheet flooring, the floor of the room must be water resistant.
b. For timber floors including particleboard, plywood and other timber based flooring materials, the floor of the room must be waterproof.
c. Tap and spout penetrations must be waterproof where they occur in horizontal surfaces.
2. For areas adjacent to non-freestanding baths and spas, the following applies:
a. Walls must be water resistant (see Figure 10.2.4a and Figure 10.2.4b).
b. Walls must be water resistant to a height of not less than 150mm above the vessel, for the extent of the vessel, where the vessel is within 75mm of a wall; and
c. Wall junctions and joints must be water resistant within 150mm above a vessel for the extent of the vessel.
3. Wall/floor junctions must be waterproof for the extent of the vessel (see Figure 10.2.4a and Figure 10.2.4b).
For inserted baths and spas, the following applies:
a. For floors and horizontal surfaces:
b. Any shelf area adjoining the bath or spa must be waterproof and include a waterstop under the vessel lip.
c. There are no requirements for the floor under a bath or spa.
b. For walls:
c. Waterproof to not less than 150mm above the lip of a bath or spa.
d. There are no requirements for the floor under a bath or spa.
c. For wall junctions and joints, the following applies:
d. Waterproof junctions within 150mm of a bath or spa.
e. There are no requirements for junctions and joints in walls beneath the lip of a bath or spa.
f. Tap and spout penetrations must be waterproof where they occur in horizontal surfaces.

Figure 10.2.4a: Areas adjacent to baths and spas without showers for concrete, compressed fibre-cement and fibre-cement sheet flooring




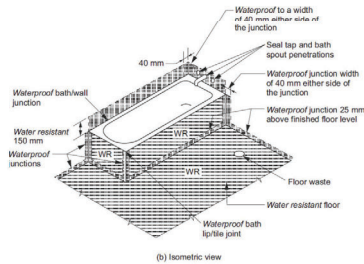



Figure 10.2.4b: Areas adjacent to baths and spas without showers for timber floors including particle-board, plywood and other floor materials

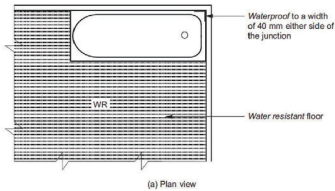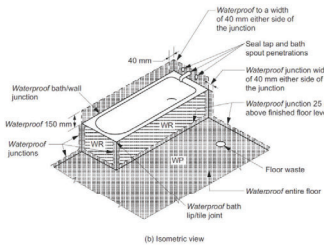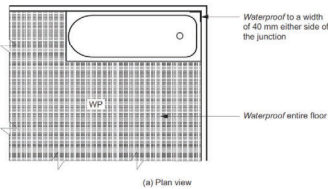

10.2.5 Other areas

1. For walls adjoining other types of vessels (e.g. sink, basin or laundry tub), the following applies:
a. Walls must be water resistant to a height of not less than 150mm above the vessel, for the extent of the vessel, where the vessel is within 75 mm of a wall (see Figure 10.2.5.)
b. Waterproof wall junctions where a vessel is fixed to a wall.
c. Waterproof tap and spout penetrations where they occur in surfaces required to be waterproof or water resistant.
2. For laundries and WCs, the following applies:
a. The floor of the room must be water resistant.
b. Wall/floor junctions must be waterproof not less than 40 mm.
c. For WCs with handheld bidet spray installations, the following applies:
d. The floor of the room must be water resistant.
e. Walls must be waterproof in WC area within a 900 mm radius from the wall connection of the handheld bidet spray device to a height of not less than 1500 mm above the floor substrate; and
f. Wall/floor junctions within the WC area within 900 mm radius from the wall connection of the handheld bidet spray device must be waterproof.
g. Wall/floor junctions within the WC area within 1000 mm radius from the wall connection of the handheld bidet spray device must be waterproof.
h. Penetrations in the WC area must be waterproof.

Figure 10.2.5: Bath and vessel abutting wall - areas to be protected

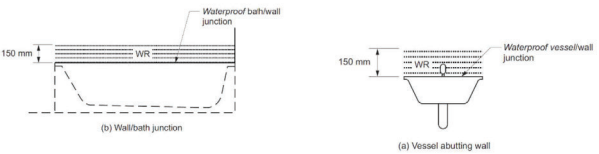

10.2.6 Waterproofing systems

1. For the purposes of this Part, a waterproofing system is deemed -
a. waterproof, if it complies with (2); or
b. water resistant, if it complies with (3).
2. For a waterproofing system required to be waterproof in accordance with 10.2.2 to 10.2.5, the materials nominated in 10.2.8 must be used.
3. For a waterproofing system required to be water resistant in accordance with 10.2.2 to 10.2.5, the materials nominated in 10.2.9 must be used in conjunction with the materials in 10.2.10.

10.2.12 Construction of wet area floors - falls

Where a floor waste is installed -
a. the minimum continuous fall of a floor plane to the waste must be 1:80; and
b. the maximum continuous fall of a floor plane to the waste must be 1:50.

REV	DATE	DESCRIPTION	BY
7	25-06-2026	230 Brick wall in Garage	
6	30-03-2026	Shower in GF Bath-Ek	



THIS DRAWING IS THE EXCLUSIVE PROPERTY OF THE DEVELOPER & THE REPRODUCTION OF ANY PART WITHOUT THE PRIOR WRITTEN CONSENT OF THE DEVELOPER IS A VIOLATION OF APPLICABLE LAWS. IN NO EVENT SHALL THE DEVELOPER BE HELD LIABLE FOR SPECIAL, COLLATERAL, INCIDENTAL OR CONSEQUENTIAL LIABILITY IN CONNECTION WITH THE USE OF THIS DIGITAL DATA ONCE RELEASED FROM THE DEVELOPERS OFFICE. THIS DRAWING IS TO BE READ & UNDERSTOOD IN CONJUNCTION WITH THE STRUCTURAL, MECHANICAL, ELECTRICAL & / OR ANY OTHER CONSULTANT'S DOCUMENTATION AS MAY BE APPLICABLE TO THE PROJECT PRIOR TO THE START OF ANY WORKS AND FOR ITS DURATION.

PROJECT:
Lot 342 36 PLEIADES STREET
36 PLEIADES STREET
AUSTRAL

DRAWING TITLE:
WATERPROOFING PLAN

NORTH:


LOT NO:	DATE:	SCALE:	DRAWING NO:	REV:
342	20-08-2026	1 : 50	CDC.16	7
DRAWN BY:	CHECKED BY:	DRAFTED BY:	CLIENT NAME:	ISSUED BY:
AS	RH	AS	Umesh Bhandari and Meena Khattri Bhandari	