

FOR CONSTRUCTION

LOT 644 - 4 WURRIDJAL STREET AUSTRAL

PROPOSED CONSTRUCTION OF A SINGLE STOREY DWELLING



BASIX COMMITMENTS		Certificate number: 1864630S Date of issue: Tuesday, 08 September 2026
WATER		
LANDSCAPE	71m2	
TOILETS	4 STARS	
KITCHEN TAPS	4 STARS	
SHOWER HEADS	4 STARS (>4.5 but <=6 Umin)	
BASIN TAPS	4 STARS	
ALTERNATIVE WATER	1500L RAINWATER TANK	
ROOF WATER TO TANK	224m2	
ALT.WATER USES- TANK	LAUNDRY	
ALT. WATER USES - RETIC	ALL TOILETS + ONE OUTDOOR TAP	
SWIMMING POOL	N/A	
ENERGY		
HOT WATER	GAS INSTANTANEOUS - 5 STAR	
AIR-CON (HEATING)	3 PHASE DUCTED - EER 3.0-3.5	
AIR-CON (COOLING)	3 PHASE DUCTED - EER 3.0-3.5	
VENTILATION - BATHROOM	NONE/ NATURAL VENTILATION	
VENTILATION - KITCHEN	DUCTED - MANUAL SWITCH	
VENTILATION - LAUNDRY	NONE/ NATURAL VENTILATION	
PV SYSTEM	N/A	
COOKTOP	GAS	
OVEN	ELECTRIC	
CLOTHES DRYING	OUTDOOR CLOTHESLINE	
LIGHTING	DEDICATED LED	

GENERAL LEGEND

AC	AIR CONDITIONING UNIT
AL	POWDERCOATED ALUMINIUM DOOR/ WINDOW
BAL	BALUSTRADE TYPE
BG	BOX GUTTER
BR1, BR2, etc.	BRICK FACE TYPE
CAP	METAL CAPPING
CD1, CD2, etc.	WALL CLADDING
CONC.	CONCRETE FLOOR
CPT	CARPET
CRT	CONCRETE ROOF TILES
CR1, CR2, etc.	CEMENT RENDER TYPE/ COLOUR
DP/S	DOWN PIPE
DW	DISH WASHER
ED	ENTRY DOOR
F	FRIDGE
FAS	FASCIA
FET	FEATURE TILE
FT, FT1, FT2, etc.	FLOOR TILES
FW	FLOOR WASTE
GD	GARAGE DOOR
GUT	GUTTER
HWU	HOT WATER UNIT
HYB	HYBRID FLOOR
L	LINEN
MR	METAL ROOF
MW	MICROWAVE OVEN
NGL	NATURAL GROUND LEVEL
OBS	OBSCURED GLASS
P	PANTRY
R	ROBE
RL	REDUCED LEVEL
RWH	RAIN WATER HEAD
RWT	RAIN WATER TANK
S	STORAGE
TOW	TOP OF WALL
TL	TIMBER LAMINATE
WC	WATER CLOSET
WM	WASHING MACHINE
SD	SMOKE DETECTOR

Sheet List				
Sheet No.	Sheet Name	Drawn By	Current Revision Date	Revision
CDC.01	COVER SHEET	AS	28-08-2026	CDC ISSUE
CDC.02A	GENERAL NOTES	AS	28-08-2026	CDC ISSUE
CDC.02B	GENERAL NOTES	AS	28-08-2026	CDC ISSUE
CDC.03	LOCATION PLAN AND SITE PLAN	AS	28-08-2026	CDC ISSUE
CDC.04	SITE ANALYSIS AND SEDIMENT CONTROL	AS	28-08-2026	CDC ISSUE
CDC.05	GROUND FLOOR PLAN	AS	17-09-2026	
CDC.06	FIRST FLOOR LEVEL	AS	28-08-2026	CDC ISSUE
CDC.07	ROOF PLAN	AS	17-09-2026	

Sheet List				
Sheet No.	Sheet Name	Drawn By	Current Revision Date	Revision
CDC.08	ELEVATION 01	AS	17-09-2026	
CDC.09	ELEVATION 02	AS	17-09-2026	
CDC.10	SECTIONS	AS	28-08-2026	CDC ISSUE
CDC.11	FLOOR AREA PLAN	AS	28-08-2026	CDC ISSUE
CDC.12	RENTABLE AREA PLAN	AS	28-08-2026	CDC ISSUE
CDC.14	COLOR SCHEDULE	AS	28-08-2026	CDC ISSUE
CDC.15	LANDSCAPE PLAN	AS	28-08-2026	CDC ISSUE
CDC.16	WATERPROOFING DETAILS	AS	28-08-2026	CDC ISSUE

NOTE: ALL IMAGES ARE FOR ILLUSTRATION ONLY AND ARE SUBJECT TO VARIATION DEPENDING ON STRUCTURAL AND FINISHING ELEMENTS AND TO AVAILABILITY OF MATERIALS.

7	28-08-2026	CDC ISSUE	
5	30-06-2026	Bar Fridge added and raked ceiling to lounge, hallway & living room-Ekta	
3	26-06-2026	Facade Updated with PVC panels - Ekta	
2	23-04-2026	Curved wall on facade and WIR, Bed2 reduce by 200mm to give space for dining, Puja nook added from WIP space - Client Meeting	
1	09-04-2026	Concept Issue	
REV	DATE	DESCRIPTION	BY

THIS DRAWING IS THE EXCLUSIVE PROPERTY OF THE DEVELOPER & THE REPRODUCTION OF ANY PART WITHOUT THE PRIOR WRITTEN CONSENT OF THE DEVELOPER IS A VIOLATION OF APPLICABLE LAWS. IN NO EVENT SHALL THE DEVELOPER BE HELD LIABLE FOR SPECIAL COLLATERAL, INCIDENTAL OR CONSEQUENTIAL LIABILITY IN CONNECTION WITH THE USE OF THIS DIGITAL DATA ONCE RELEASED FROM THE DEVELOPER'S OFFICE. THIS DRAWING IS TO BE READ & UNDERSTOOD IN CONJUNCTION WITH THE STRUCTURAL, MECHANICAL, ELECTRICAL & / OR ANY OTHER CONSULTANT'S DOCUMENTATION AS MAY BE APPLICABLE TO THE PROJECT PRIOR TO THE START OF ANY WORKS AND FOR ITS DURATION.

PROJECT:
LOT 644 WURRIDJAL STREET
LOT 644 4 WURRIDJAL STREET
AUSTRAL 2179

DRAWING TITLE:
COVER SHEET

NORTH:

LOT NO: 644	DATE: 18-09-2026	SCALE: As indicated	<u>DRAWING</u> No: CDC.01	<u>REV:</u> 7
DRAWN BY: AS	CHECKED BY: RH			ISSUED BY:
DRAFTED BY: RS	CLIENT NAME: Anish KC and Deepa Basnet			

BUILDING SPECIFICATIONS

National Construction Code – Volume 2, Amendment 1 – Building Code of Australia 2022 & Housing Provisions Standard 2022

SITE PREPARATION

- PART 3.1 OF THE NCC VOLUME 2, AMENDMENT 1 - BUILDING CODE OF AUSTRALIA 2022 & HOUSING PROVISIONS STANDARD 2022.

EARTHWORKS

- TO BE CARRIED OUT IN ACCORDANCE WITH THE REQUIREMENTS OF THE ENVIRONMENTAL PLANNING & ASSESSMENT ACT 1979 AND DEVELOPMENT CONSENT CONDITIONS
- PART 3.2 OF THE NCC VOLUME 2, AMENDMENT 1 - BUILDING CODE OF AUSTRALIA 2022 & HOUSING PROVISIONS STANDARD 2022.
- AS 4678:2002 - EARTH-RETAINING STRUCTURES

DRAINAGE

- PART 3.3 OF THE NCC VOLUME 2, AMENDMENT 1 - BUILDING CODE OF AUSTRALIA 2022 & HOUSING PROVISIONS STANDARD 2022.
- AS/NZS 3500.1:2021 - PLUMBING & DRAINAGE - WATER SERVICES
- AS/NZS 3500.2:2021 - PLUMBING & DRAINAGE - SANITARY PLUMBING & DRAINAGE
- AS/NZS 3500.3:2021 - PLUMBING & DRAINAGE - STORMWATER DRAINAGE
- AS/NZS 3500.4:2021 - PLUMBING & DRAINAGE - HEATED WATER SERVICES

STRUCTURAL WORK

- Part 2.2 OF THE NCC VOLUME 2, AMENDMENT 1 - BUILDING CODE OF AUSTRALIA 2022 & HOUSING PROVISIONS STANDARD 2022.
- AS 4100:2020 - STEEL STRUCTURES CODES
- AS/NZS 1170.0:2002 - GENERAL PRINCIPLES
- AS/NZS 1170.1:2002 - PARTS 1 PERMANENT, IMPOSED AND OTHER ACTIONS
- AS/NZS 1170.2:2021 - PART 2 WIND ACTIONS
- AS 3700:2018 - SAA MASONRY CODE
- AS 1684.3:2021 - RESIDENTIAL TIMBER FRAMED CONSTRUCTION

FOOTINGS & SLABS

- PART 4 OF THE NCC VOLUME 2, AMENDMENT 1 - BUILDING CODE OF AUSTRALIA 2022 & HOUSING PROVISIONS STANDARD 2022.
- AS 2159:2009 - PILING - DESIGN & INSTALLATION
- AS 2870:2011 - RESIDENTIAL SLABS & FOOTINGS
- AS 3600:2018 - CONCRETE STRUCTURES

MASONRY

- PART 5 OF THE NCC VOLUME 2, AMENDMENT 1 - BUILDING CODE OF AUSTRALIA 2022 & HOUSING PROVISIONS STANDARD 2022.

- AS 3700:2018 - MASONRY STRUCTURES

FRAMING

- PART 6 OF THE NCC VOLUME 2, AMENDMENT 1 - BUILDING CODE OF AUSTRALIA 2022 & HOUSING PROVISIONS STANDARD 2022.

- AS 1684.2:2021 - RESIDENTIAL TIMBER-FRAMED CONSTRUCTION - NON- CYCLONIC AREAS
- AS 1720.1:2010 - TIMBER STRUCTURES - DESIGN METHODS
- AS 4100:2020 - STEEL STRUCTURES
- AS 3660.1:2014 - TERMITE MANAGEMENT SYSTEM

ROOF & WALL CLADDING

- PART 7 OF THE NCC VOLUME 2, AMENDMENT 1 - BUILDING CODE OF AUSTRALIA 2022 & HOUSING PROVISIONS STANDARD 2022.
- AS 1273:1991 - UNPLASTICIZED PVC (UPVC) DOWNPIPES & FITTINGS FOR RAINWATER
- AS 1562.1:2018 - DESIGN & INSTALLATION OF SHEET ROOF & WALL CLADDING - METAL
- AS/NZS 1562.3:2006 - DESIGN & INSTALLATION OF SHEET ROOF & WALL CLADDING - PLASTIC
- AS 2049:2002 - ROOF TILES
- AS 2050:2018 - INSTALLATION OF ROOF TILES
- AS 4285:2019 - ROOFLIGHTS

GLAZING

- PART 8 OF THE NCC VOLUME 2, AMENDMENT 1 - BUILDING CODE OF AUSTRALIA 2022 & HOUSING PROVISIONS STANDARD 2022.
- AS 1288:2021 - GLASS IN BUILDINGS - SELECTION & INSTALLATION
- AS 2047:2014 - WINDOWS & EXTERNAL GLAZED DOORS IN BUILDINGS
- AS/NZS 2208:1996 - SAFETY GLAZING MATERIALS IN BUILDINGS

FIRE SAFETY

- PART 9 OF THE NCC VOLUME 2, AMENDMENT 1 - BUILDING CODE OF AUSTRALIA 2022 & HOUSING PROVISIONS STANDARD 2022.
- AS 3786:2014 - SMOKE ALARMS USING SCATTERED LIGHT, TRANSMITTED LIGHT OR IONIZATION

HEALTH & AMENITY

- PART 10 OF THE NCC VOLUME 2, AMENDMENT 1 - BUILDING CODE OF AUSTRALIA 2022 & HOUSING PROVISIONS STANDARD 2022.
- AS/NZS ISO 717.1:2004 - ACOUSTICS - RATING OF SOUND INSULATION IN BUILDINGS & OF BUILDING ELEMENTS - AIRBORNE SOUND INSULATION
- AS ISO 717.2:2004 - ACOUSTICS - RATING OF SOUND INSULATION IN BUILDINGS & OF BUILDING ELEMENTS - IMPACT SOUND INSULATION
- AS 1668.2:2012 - THE USE OF VENTILATION & AIR CONDITIONING IN BUILDINGS - MECHANICAL VENTILATION IN BUILDINGS
- AS 1668.4:2012 - THE USE OF VENTILATION & AIR CONDITIONING IN BUILDINGS - NATURAL VENTILATION OF BUILDINGS
- AS/NZS 1680.0:2009 - INTERIOR LIGHTING - SAFE MOVEMENT
- AS 3740:2021 - WATERPROOFING OF DOMESTIC WET AREAS
- AS 3000:2018 - ELECTRICAL INSTALLATION
- BCA Part 10.8.1, AS4200.1 & AS4200.2 - PLIABLE BUILDING MEMBRANE INSTALLED.

WATERPROOFING

- PART 10.2 OF THE NCC VOLUME 2, AMENDMENT 1 - BUILDING CODE OF AUSTRALIA 2022 & HOUSING PROVISIONS STANDARD 2022
- AS 3740:2021 - WATERPROOFING TO WET AREA
- AS 4654:2012 - EXTERNAL WET AREAS

SAFE MOVEMENT & ACCESS

- PART 11 OF THE NCC VOLUME 2, AMENDMENT 1 - BUILDING CODE OF AUSTRALIA 2022 & HOUSING PROVISIONS STANDARD 2022.
- AS 1428.1:2009 - DESIGN FOR ACCESS & MOBILITY - GENERAL REQUIREMENTS FOR ACCESS - NEW BUILDING WORK
- AS 1657:2018 - FIXED PLATFORMS, WALKWAYS, STAIRWAYS & LADDERS - DESIGN, CONSTRUCTION & INSTALLATION

HANDRAILS & BALUSTRADE

- PART 11.3.3 OF THE NCC VOLUME 2, AMENDMENT 1 - BUILDING CODE OF AUSTRALIA 2022 & HOUSING PROVISIONS STANDARD 2022.
- PART 11.3.4 OF THE NCC VOLUME 2, AMENDMENT 1 - BUILDING CODE OF AUSTRALIA 2022 & HOUSING PROVISIONS STANDARD 2022.
- PART 11.3.5 OF THE NCC VOLUME 2, AMENDMENT 1 - BUILDING CODE OF AUSTRALIA 2022 & HOUSING PROVISIONS STANDARD 2022.
- AS 1170.1:2002 - BALUSTRADE INSTALLATION

PROTECTION OF OPENABLE WINDOW

- PART 11.3.7 AND 11.3.8 OF THE NCC VOLUME 2, AMENDMENT 1 - BUILDING CODE OF AUSTRALIA 2022 & HOUSING PROVISIONS STANDARD 2022.

ENERGY EFFICIENCY

- PART 13 OF THE NCC VOLUME 2, AMENDMENT 1 - BUILDING CODE OF AUSTRALIA 2022 & HOUSING PROVISIONS STANDARD 2022 & BASIX CERTIFICATE.

MECHANICAL VENTILATION

- EXHAUST FROM A BATHROOM, SANITARY COMPARTMENT TO DISCHARGE DIRECTLY TO OUTDOOR AIR WITH MINIMUM FLOW RATE OF 25L/S & MAKE-UP AIR VIA OPENINGS TO AN ADJACENT ROOM WITH A FREE AREA OF 14,000 MM². THIS EXHAUST SYSTEM MUST BE INTERLOCKED WITH LIGHT SWITCH AND INCLUDE RUN-ON TIMER SO THAT THE EXHAUST SYSTEM CONTINUES TO OPERATE FOR 10 MINUTES AFTER THE LIGHT SWITCH IS OFF.
- ANY INSTALLED - KITCHEN RANGEHOOD EXHAUST TO DISCHARGE DIRECTLY OR VIA DUCT TO OUTDOOR AIR WITH MINIMUM FLOW RATE OF 40L/S & MAKE-UP AIR VIA OPENINGS TO AN ADJACENT ROOM WITH A FREE AREA OF 14,000 MM².
- LAUNDRY EXHAUST TO DISCHARGE DIRECTLY OR VIA DUCT TO OUTDOOR AIR WITH MINIMUM FLOW RATE OF 40L/S & MAKE-UP AIR VIA OPENINGS TO AN ADJACENT ROOM WITH A FREE AREA OF 14,000 MM².



REV	DATE	DESCRIPTION	BY
7	28-08-2026	CDC ISSUE	



THIS DRAWING IS THE EXCLUSIVE PROPERTY OF THE DEVELOPER & THE REPRODUCTION OF ANY PART WITHOUT THE PRIOR WRITTEN CONSENT OF THE DEVELOPER IS A VIOLATION OF APPLICABLE LAWS. IN NO EVENT SHALL THE DEVELOPER BE HELD LIABLE FOR SPECIAL COLLATERAL, INCIDENTAL OR CONSEQUENTIAL LIABILITY IN CONNECTION WITH THE USE OF THIS DIGITAL DATA ONCE RELEASED FROM THE DEVELOPER'S OFFICE. THIS DRAWING IS TO BE READ & UNDERSTOOD IN CONJUNCTION WITH THE STRUCTURAL, MECHANICAL, ELECTRICAL & / OR ANY OTHER CONSULTANT'S DOCUMENTATION AS MAY BE APPLICABLE TO THE PROJECT PRIOR TO THE START OF ANY WORKS AND FOR ITS DURATION.

PROJECT:
LOT 644 WURRIDJAL STREET
LOT 644 4 WURRIDJAL STREET
AUSTRAL 2179

DRAWING TITLE:
GENERAL NOTES

NORTH:

LOT NO: 644	DATE: 18-09-2026	SCALE: 1 : 2	<u>DRAWING</u> No: CDC.02A	<u>REV:</u> 7
DRAWN BY: AS	CHECKED BY: RH	ISSUED BY:		
DRAFTED BY: RS	CLIENT NAME: Anish KC and Deepa Basnet			

TERMITE SHEET


- TERMITE SHEET EXTENDS THROUGH THE ENTIRE MASONRY LEAF AND IS VISIBLE AT THE FINISHED FACE OF THE WALL.



FIGURE 5.5 (in part) TYPICAL SHEET INSTALLATION TO EXTERNAL WALL WITH CONCRETE FLOOR SLAB

DPC FOR BRICKS

DAMP-PROOF COURSE (DPC) TO EXTENDS THROUGH THE ENTIRE MASONRY LEAF AND NEED TO BE VISIBLE AT THE FINISHED FACE OF THE WALL FROM OUTSIDE

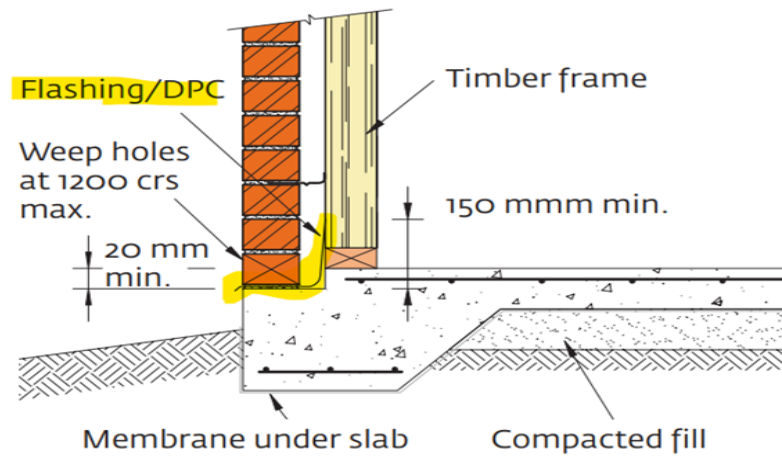

WATERPROOFING

FALL TO FLOOR WASTE TO BE MINIMUM 1:80 TO MAXIMUM 1:50

Figure 10.2.29: Typical membrane termination at drainage outlet


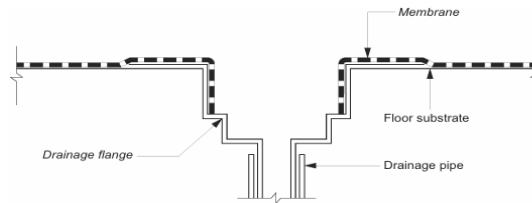



Figure 10.2.24: Typical bathroom door details for whole bathroom waterproofing

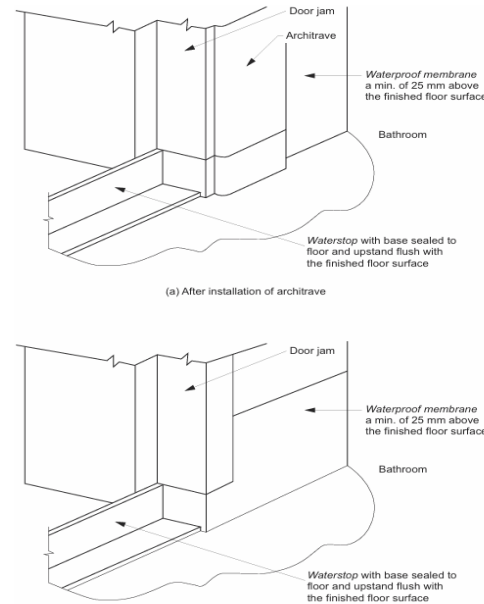


BASIN & BATHTUB:

Figure 10.2.5:

Bath and vessel abutting wall — areas to be protected

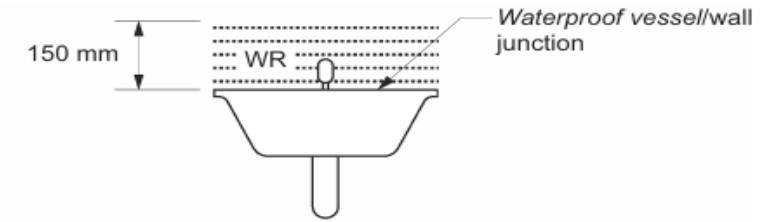

(a) Vessel abutting wall

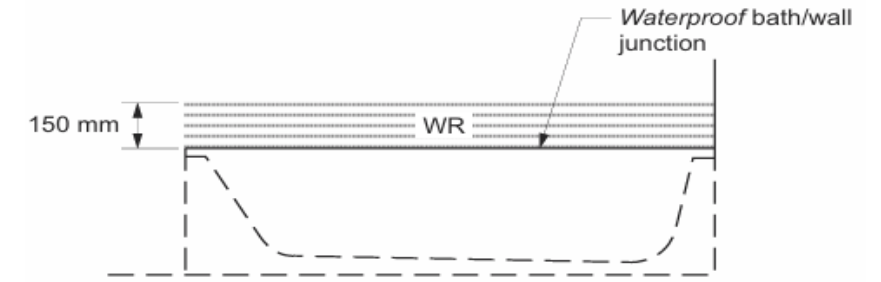


(b) Wall/bath junction


ENCLOSED SHOWER AREA

Figure 10.2.17:

Typical hobless construction

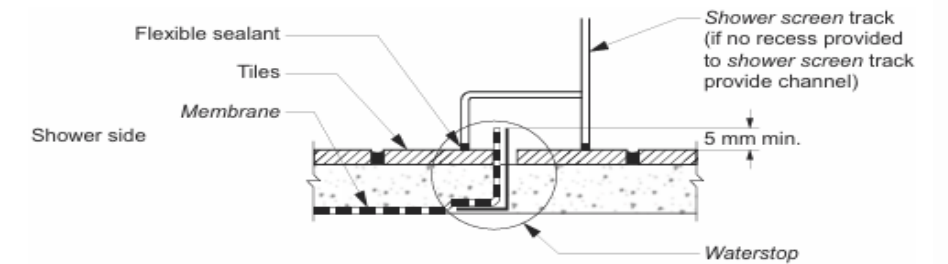

Extent of treatment for shower areas — concrete compressed fibre-cement and fibre-cement sheet floors

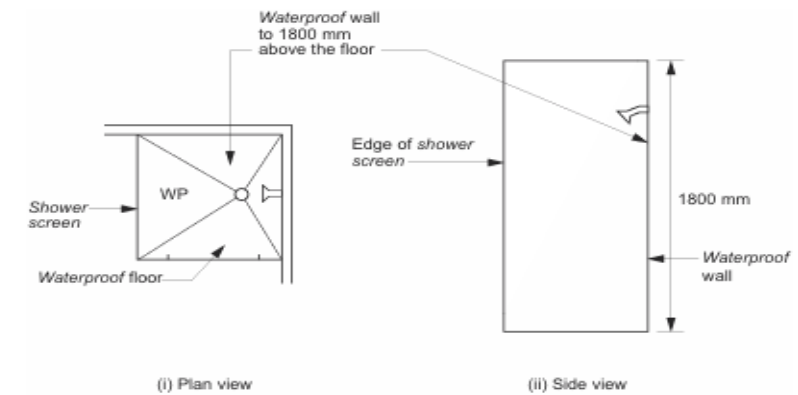

(a) Enclosed shower

REV	DATE	DESCRIPTION	BY
7	28-08-2026	CDC ISSUE	



RUBY HOMES

THIS DRAWING IS THE EXCLUSIVE PROPERTY OF THE DEVELOPER & THE REPRODUCTION OF ANY PART WITHOUT THE PRIOR WRITTEN CONSENT OF THE DEVELOPER IS A VIOLATION OF APPLICABLE LAWS. IN NO EVENT SHALL THE DEVELOPER BE HELD LIABLE FOR SPECIAL COLLATERAL, INCIDENTAL OR CONSEQUENTIAL LIABILITY IN CONNECTION WITH THE USE OF THIS DIGITAL DATA ONCE RELEASED FROM THE DEVELOPER'S OFFICE. THIS DRAWING IS TO BE READ & UNDERSTOOD IN CONJUNCTION WITH THE STRUCTURAL, MECHANICAL, ELECTRICAL & / OR ANY OTHER CONSULTANT'S DOCUMENTATION AS MAY BE APPLICABLE TO THE PROJECT PRIOR TO THE START OF ANY WORKS AND FOR ITS DURATION.


PROJECT:
LOT 644 WURRIDJAL STREET
LOT 644 4 WURRIDJAL STREET
AUSTRAL 2179

DRAWING TITLE:
GENERAL NOTES

NORTH:


LOT NO:	DATE:	SCALE:	DRAWING No:	REV:
644	18-09-2026	1 : 2	CDC.02B	7
DRAWN BY:	CHECKED BY:	CLIENT NAME:	ISSUED BY:	
AS	RH	Anish KC and Deepa Basnet		
DRAFTED BY:				
RS				

CDC ISSUE

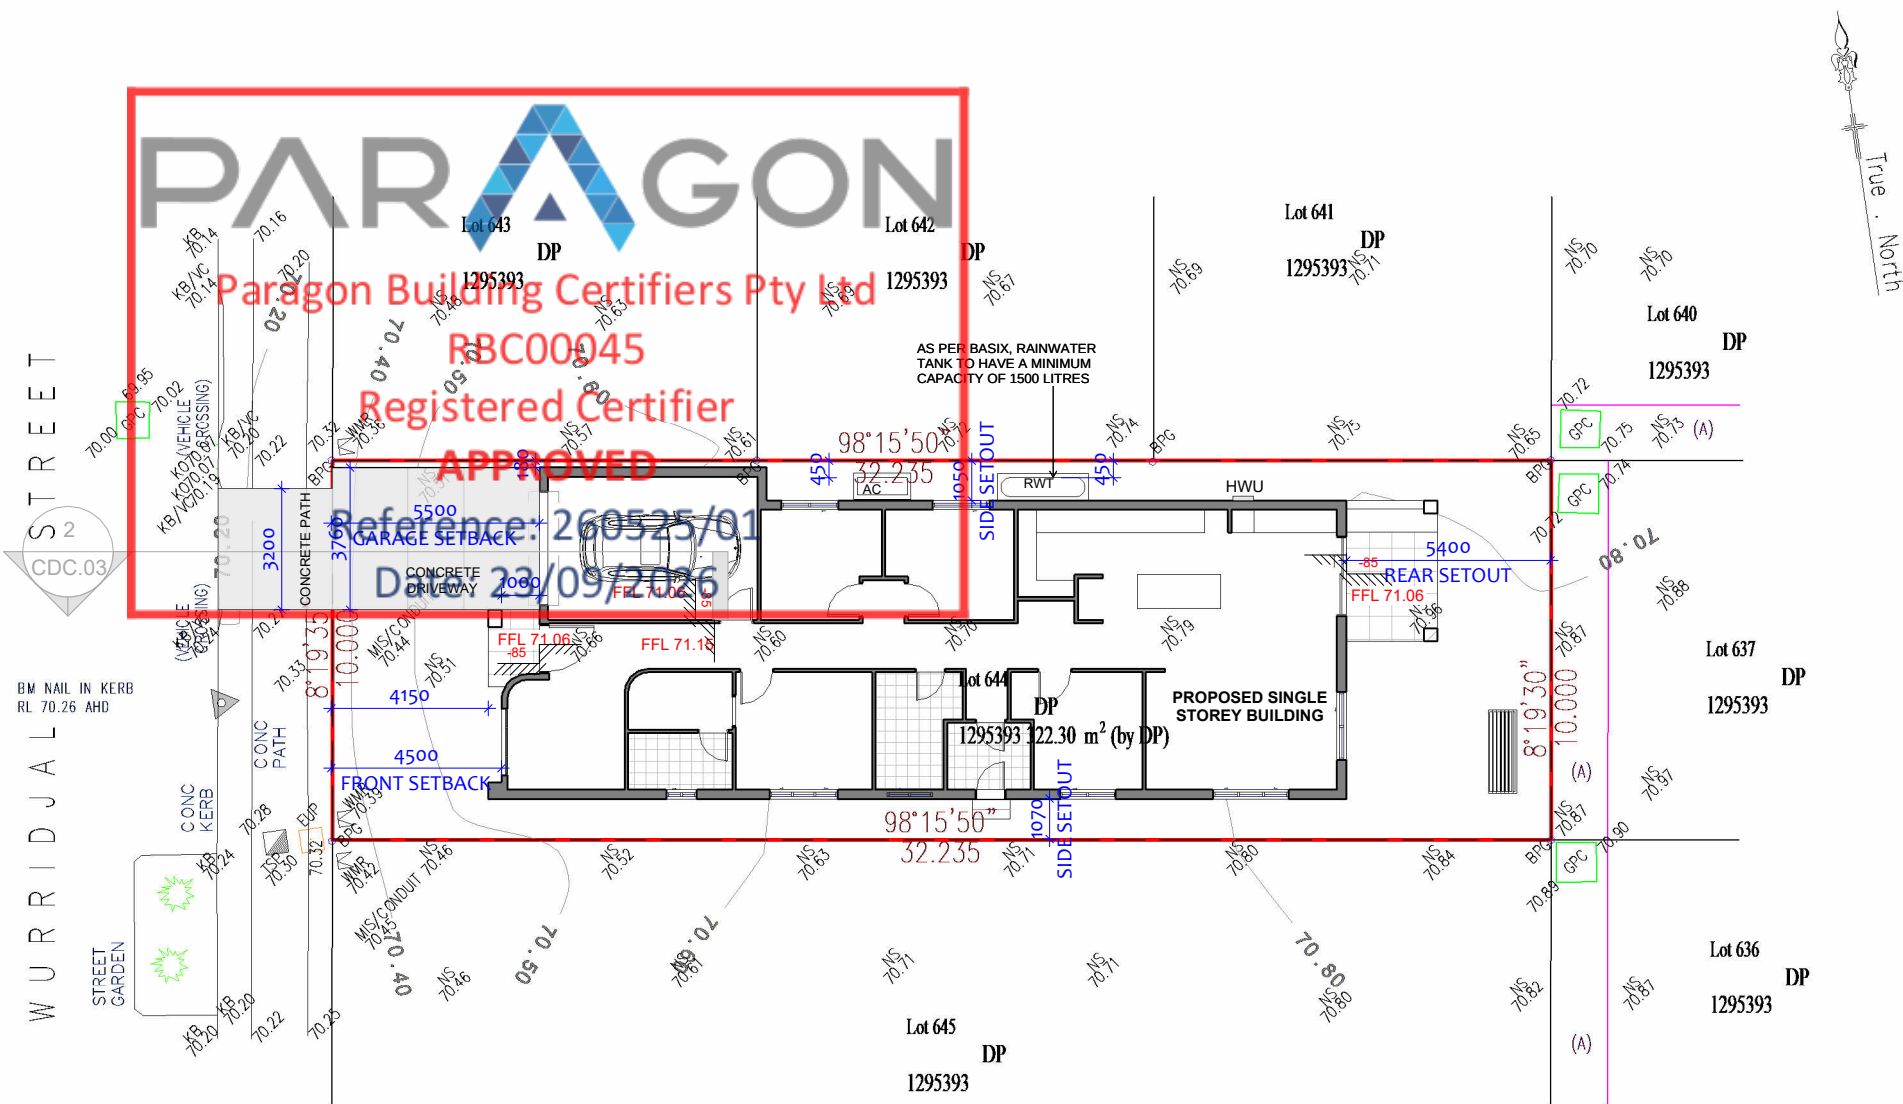

CDC - SITE PLAN

1 : 200

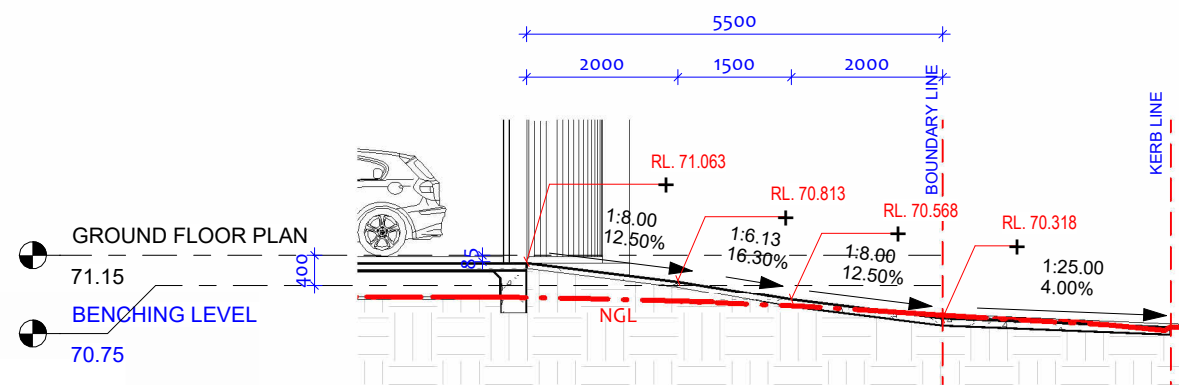

DRIVEWAY SECTION

2 : 100

AREA SCHEDULE (RENTABLE)	
NAME	AREA (m2)
LOT AREA	322.3
GROUND FLOOR	141
GARAGE	21
PRIVATE OPEN SPACE	16
DRIVEWAY	21.67
FRONT LANDSCAPE	25.9
REAR LANDSCAPE	45.12

GREENFIELD HOUSING CODE COMPLIANCE TABLE

DESCRIPTION		COMPLIANCE		COMMENT
ELEMENT	CODE CONTROL	REQUIREMNT	PROPOSED	
LOAND ZONE	1 GENERAL RESIDENTIAL			
LOT NO	LOT 644			
LOT AREA	322.30 m2			
LOT WIDTH	Standard Lot Min. 6m at Building Line facing primary road	6.0m	10 m	YES
HEIGHT	MAX. Height	8.5m	5.2m (MAX.)	YES
FRONT SETBACK	FRONT SET BACK (Min. Setback from Primary Road) For 300-350 sqm. Lot	4.5 m	4.5m	YES
REAR SET BACK (MIN.)	GROUND FLOOR	3m	5.4m	YES
SIDE SET BACK (MIN.)	GROUND FLOOR	0/0.9m	.18/1.07m	YES
FLOOR SPACE RATIO (FSR)	235 sqm.	235.00m2	144 m2	YES
GROSS FLOOR AREA PLAN	GROUND FLOOR		141 m2	YES
	FIRST FLOOR		NA	YES
TOTAL FLOOR AREA			162 m2	YES
ROOF AREA			224 m2	YES
GARAGE			23	YES
PRIVATE OPEN SPACE	>10m Lot width	16m2	16 m2	YES
LANDSCAPE AREA	15 % of TOTAL LAND AREA	50.4 m2	70.1 m2	YES

CDC ISSUE


REV	DATE	DESCRIPTION	BY
7	28-08-2026	CDC ISSUE	

RUBY HOMES

THIS DRAWING IS THE EXCLUSIVE PROPERTY OF THE DEVELOPER & THE REPRODUCTION OF ANY PART WITHOUT THE PRIOR WRITTEN CONSENT OF THE DEVELOPER IS A VIOLATION OF APPLICABLE LAWS. IN NO EVENT SHALL THE DEVELOPER BE HELD LIABLE FOR SPECIAL COLLATERAL, INCIDENTAL OR CONSEQUENTIAL LIABILITY IN CONNECTION WITH THE USE OF THIS DIGITAL DATA ONCE RELEASED FROM THE DEVELOPER'S OFFICE. THIS DRAWING IS TO BE READ & UNDERSTOOD IN CONJUNCTION WITH THE STRUCTURAL, MECHANICAL, ELECTRICAL & / OR ANY OTHER CONSULTANT'S DOCUMENTATION AS MAY BE APPLICABLE TO THE PROJECT PRIOR TO THE START OF ANY WORKS AND FOR ITS DURATION.

PROJECT:
LOT 644 WURRIDJAL STREET
LOT 644 4 WURRIDJAL STREET
AUSTRAL 2179

DRAWING TITLE:
LOCATION PLAN AND SITE PLAN

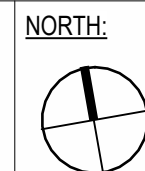

LOT NO: 644	DATE: 18-09-2026	SCALE: As indicated	DRAWING No: CDC.03	REV: 7
DRAWN BY: AS	CHECKED BY: RH		ISSUED BY:	
DRAFTED BY: RS	CLIENT NAME: Anish KC and Deepa Basnet			







CDC - SITE ANALYSIS AND SEDIMENTATION

1 : 200

SD 5-7 STABILISED SITE ACCESS

- 1) STRIP TOPSOIL AND LEVEL SITE.
- 2) COMPACT SUBGRADE.
- 3) COVER AREA WITH GEOTEXILE.
- 4) CONSTRUCT 200 mm THICK PAD OVER GEOTEXILE USING ROADBASE OR 30 mm AGGREGATE. Min 15 m LONG OR TO BUILDING ALIGNMENT. Min 3 m WIDE.
- 5) CONSTRUCT HUMPS IMMEDIATELY WITHIN BOUNDARY TO DIVERT WATER TO A SEDIMENT FENCE OR OTHER SEDIMENT TRAP.

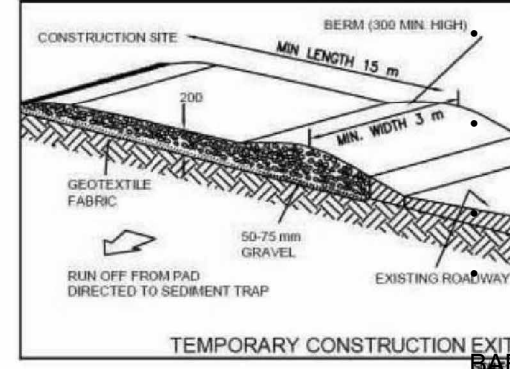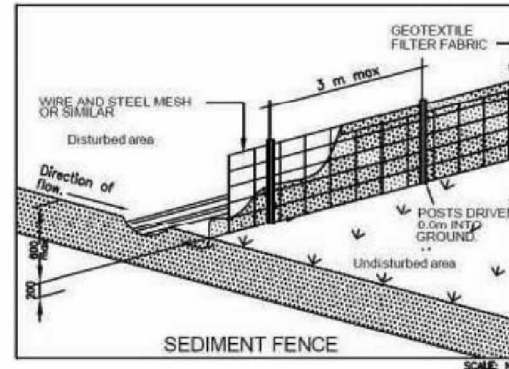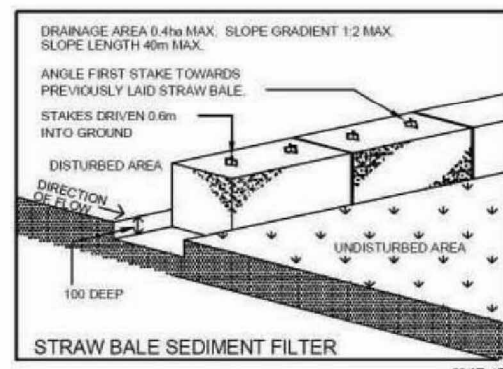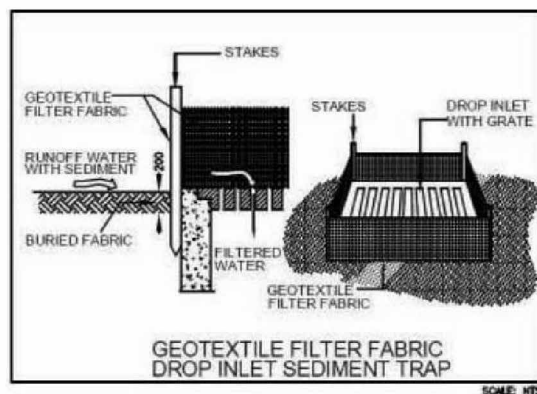

SEDIMENT FENCE

TEMPORARY CONSTRUCTION EXIT

TEMPORARY 1.8M HIGH WIRE ML FENCE WITH DUSTPROOF MESH APPLIED TO FULL HEIGHT TO BOUNDARIES AS REQUIRED

LOCATION OF WASTE BINS

SEDIMENT FENCE AS REQUIRED

GRAVEL ACCESS

SITE ACCESS AREA TO BE USED FOR WASHDOWN AREA

FOOTPATH CLEAN AND CLEAR AT ALL TIMES

LOCATION OF STOCKPILE MATERIAL

MATERIAL STORAGE AREA

TEMPORARY TOILETS

INSTALL TEMPORARY SEDIMENT BARRIERS TO ALL INLET PITS LIKELY TO COLLECT SILT LADEN WATER, TO COUNCIL'S REQUIREMENTS.

SD 6-9 GEOTEXTILE INLET FILTER

- 1) FABRICATE A SEDIMENT BARRIER MADE FROM GEOTEXILE. REFER SD6-7 FOR DETAILS.
- 2) SUPPORT GEOTEXILE WITH MESH TIED TO POSTS AT 1 m Ctrs.
- 3) DO NOT COVER INLET WITH GEOTEXILE.

SITE WORKS NOTES

1. ORIGIN OF LEVELS PROVIDED BY SURVEYOR

2. THE BUILDER SHALL VERIFY ALL DIMENSIONS AND EXISTING LEVELS ON SITE PRIOR TO THE COMMENCEMENT OF WORK AND ANY DISCREPANCIES SHALL BE REPORTED TO THE SURVEYOR / ENGINEER.

3. TOPSOIL SHALL BE STRIPPED FROM THE CONSTRUCTION AREA AND STOCKPILED ON SITE, TO BE LATER SPREAD OR DISPOSED OFF SITE AS DIRECTED BY SUPERVISOR / ENGINEER.

4. ALL TRENCH BACKFILL MATERIAL SHALL BE COMPACTED TO THE SAME DENSITY AS THE ADJACENT MATERIAL.

5. ALL SERVICE TRENCHES UNDER VEHICULAR PAVEMENTS SHALL BE BACKFILLED WITH SAND OR APPROVED GRANULAR MATERIALS, TO THE UNDERSIDE OF THE PAVEMENT, AND COMPACTED TO 98% STANDARD MAXIMUM DRY DENSITY, IN ACCORDANCE WITH AS 1289E1.1.

SEDIMENT AND EROSION NOTES:

- THIS PLAN TO BE READ IN CONJUNCTION WITH SEDIMENT AND EROSION CONTROL DETAILS AS ATTACHED.
- THE CONTRACTOR SHALL IMPLEMENT ALL SOIL EROSION AND SEDIMENT CONTROL MEASURES AS NECESSARY AND TO THE SATISFACTION OF COUNCIL PRIOR TO THE COMMENCEMENT AND DURING CONSTRUCTION. NO DISTURBANCE TO THE SITE SHALL BE PERMITTED OTHER THAN IN THE IMMEDIATE AREA OF THE WORK AND NO MATERIAL SHALL BE REMOVED FROM THE SITE WITHOUT COUNCIL'S APPROVAL. ALL SEDIMENT AND EROSION CONTROL DEVICES TO BE INSTALLED AND MAINTAINED IN ACCORDANCE WITH STANDARDS OUTLINED IN NSW DEPARTMENT OF HOUSING "MANAGING URBAN STORMWATER-SOILS AND CONSTRUCTIONS".
- TOPSOIL SHALL BE STRIPPED AND STOCKPILED OUTSIDE HAZARD AREAS SUCH AS DRAINAGE LINES. THIS TOP SOIL IS TO BE RESPIRED LATER ON AREAS TO BE REVEGETATED AND STABILISED ONLY. (I.E ALL FOOTPATHS, BATTERS, SITE REGARDING AREAS, BASINS AND CATCH DRAINS). TOPSOIL SHALL NOT BE RESPIRED ON ANY OTHER AREAS UNLESS SPECIALLY INSTRUCTED BY THE SUPERIDENT. IF THEY ARE TO REMAIN FOR LONGER THAN ONE MONTH STOCKPILES SHALL BE PROTECTED FROM EROSION BY COVERING THEM WITH A MULCH AND HYDROSEEDING AND, IF NECESSARY, BY LOCATING BANKS OR DRAINS DOWNSTREAM OF A STOCKPILE TO RETARD SILT LADEN RUNOFF.
- THE CONTRACTOR SHALL REGULARLY MAINTAIN ALL SEDIMENT AND EROSION CONTROL DEVICES AND REMOVE ACCUMULATED SILT FROM SUCH DEVICES SUCH THAT MORE THAN 60% OF THEIR CAPACITY LOST. ALL THE SILTS TO BE PLACED OUTSIDE THE LIMIT OF WORKS. THE PERIOD FOR MAINTAINING THESE DEVICES SHALL BE AT LEAST UNTIL ALL DISTURBED AREAS ARE REVEGETATED AND FURTHER AS MAY BE DIRECTED BY THE SUPERINTENDENT OR COUNCIL.
- LAY TURF STRIP (MIN 300 mm WIDE) ON 100 mm TOPSOIL WITH 1.0 m LONG RETURNS EVERY 6.0m BEHIND ALL KERB AT THE TOP OF ALL BATTERS AND AROUND STRUCTURES IMMEDIATELY AFTER BACKFILLING OR FORMATION.
- THE CONTRACTOR SHALL GRASS SEED ALL DISTURBED AREAS WITH AN APPROVED MIX AS SHOWN AS PRACTICABLE AFTER COMPLETION OF EARTHWORKS AND REGRADING.
- VEHICULAR TRAFFIC SHALL BE CONTROLLED DURING CONSTRUCTION CONFINING ACCESS WHERE POSSIBLE TO NOMINATED STABILISED ACCESS POINTS.
- WHEN ANY DEVICES ARE TO BE HANDED OVER TO COUNCIL, THEY SHALL BE IN CLEAN AND STABLE CONDITION.
- THE CONTRACTOR SHALL IMPLEMENT DUST CONTROL BY REGULAR WETTING DOWN (BUT NOT SATURATING) DISTURBED AREA.
- PROVIDE AND MAINTAIN SILT TRAPS AROUND ALL SURFACE INLET PITS UNTIL CATCHMENT IS REVEGETATED OR PAVED.
- REVEGETATE ALL TRENCHES IMMEDIATELY UPON COMPLETION OF BACKFILLING.
- ALL DRAINAGE PIPE INLETS TO BE CAPPED UNTIL:
 - A) DOWNPIPES CONNECTED
 - B) PITS CONSTRUCTED & PROTECTED WITH SILT

CDC ISSUE

REV	DATE	DESCRIPTION	BY
7	28-08-2026	CDC ISSUE	

RUBY HOMES

THIS DRAWING IS THE EXCLUSIVE PROPERTY OF THE DEVELOPER & THE REPRODUCTION OF ANY PART WITHOUT THE PRIOR WRITTEN CONSENT OF THE DEVELOPER IS A VIOLATION OF APPLICABLE LAWS. IN NO EVENT SHALL THE DEVELOPER BE HELD LIABLE FOR SPECIAL COLLATERAL, INCIDENTAL OR CONSEQUENTIAL LIABILITY IN CONNECTION WITH THE USE OF THIS DIGITAL DATA ONCE RELEASED FROM THE DEVELOPER'S OFFICE. THIS DRAWING IS TO BE READ & UNDERSTOOD IN CONJUNCTION WITH THE STRUCTURAL, MECHANICAL, ELECTRICAL & / OR ANY OTHER CONSULTANT'S DOCUMENTATION AS MAY BE APPLICABLE TO THE PROJECT PRIOR TO THE START OF ANY WORKS AND FOR ITS DURATION.


PROJECT:
LOT 644 WURRIDJAL STREET
LOT 644 4 WURRIDJAL STREET
AUSTRAL 2179

DRAWING TITLE:
SITE ANALYSIS AND SEDIMENT CONTROL




LOT NO:	DATE:	SCALE:	DRAWING No:	REV:
644	18-09-2026	As indicated	CDC.04	7
DRAWN BY:	CHECKED BY:	CLIENT NAME:	ISSUED BY:	
AS	RH	Anish KC and Deepa Basnet		

DIMENSIONS SHOWN ARE STRUCTURAL MEASUREMENTS ONLY
FINAL MEASUREMENTS MAY VARY DEPENDING ON GYPROCK, TILE
BEDDING, SCREEDING AND SITE CONDITIONS AND STRUCTURAL
ELEMENTS.

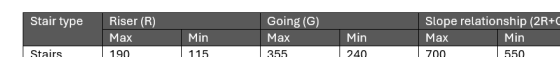

8	17-09-2026	Roof Updated	
7	28-08-2026	CDC ISSUE	
6	2-07-2026	Front windows curved - Sudeep	
5	30-06-2026	Bar Fridge added and raked ceiling to lounge, hallway & living room-Ekta	
2	23-04-2026	Curved wall on facade and WIR, Bed2 reduce by 200mm to give space for dining, Puja nook added from WIP space - Client Meeting	
REV	DATE	DESCRIPTION	BY

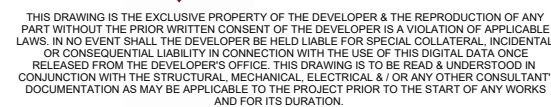


NORTH:



LOT NO: 644	DATE: 18-09-2026	SCALE: 1 : 100	<u>DRAWING</u> No:	<u>REV:</u> 8
DRAWN BY: AS	CHECKED BY: RH		CDC.05	ISSUED BY:
DRAFTED BY: RS	CLIENT NAME: Anish KC and Deepa Basnet			

IMPORTANT NOTES:
ALL DIMENSIONS AND NOTES ON ALL PLANS MUST BE CHECKED AND VERIFIED BY BUILDERS AND OWNER PRIOR TO COMMENCEMENT OF ANY BUILDING WORKS. TO CLARIFY AND CONFIRM WITH CONSTRUCTION COMPANY FOR DISCREPANCIES ON ALL DOCUMENTS AND PLANS PROVIDED FOR CONSTRUCTION. ANY WORK INDICATED ON THE PLAN BUT NOT IN THE SPECIFICATION BUT WHICH IS NECESSARY AS PART OF THE CONTRACT, VARIATION TO PLANS, SPECIFICATIONS MAY NOT BE MADE WITHOUT THE WRITTEN CONSENT OF OWNER. IT IS THE RESPONSIBILITY OF THE BUILDER/END USER TO VERIFY PLANS AND SPECIFICATIONS AS TO THEIR ACCURACY AND COMPLY CURRENT BCA AND AUSTRALIAN STANDARDS. WINDOWS TO COMPLY WITH 3.9.3.5 OF THE BCA.

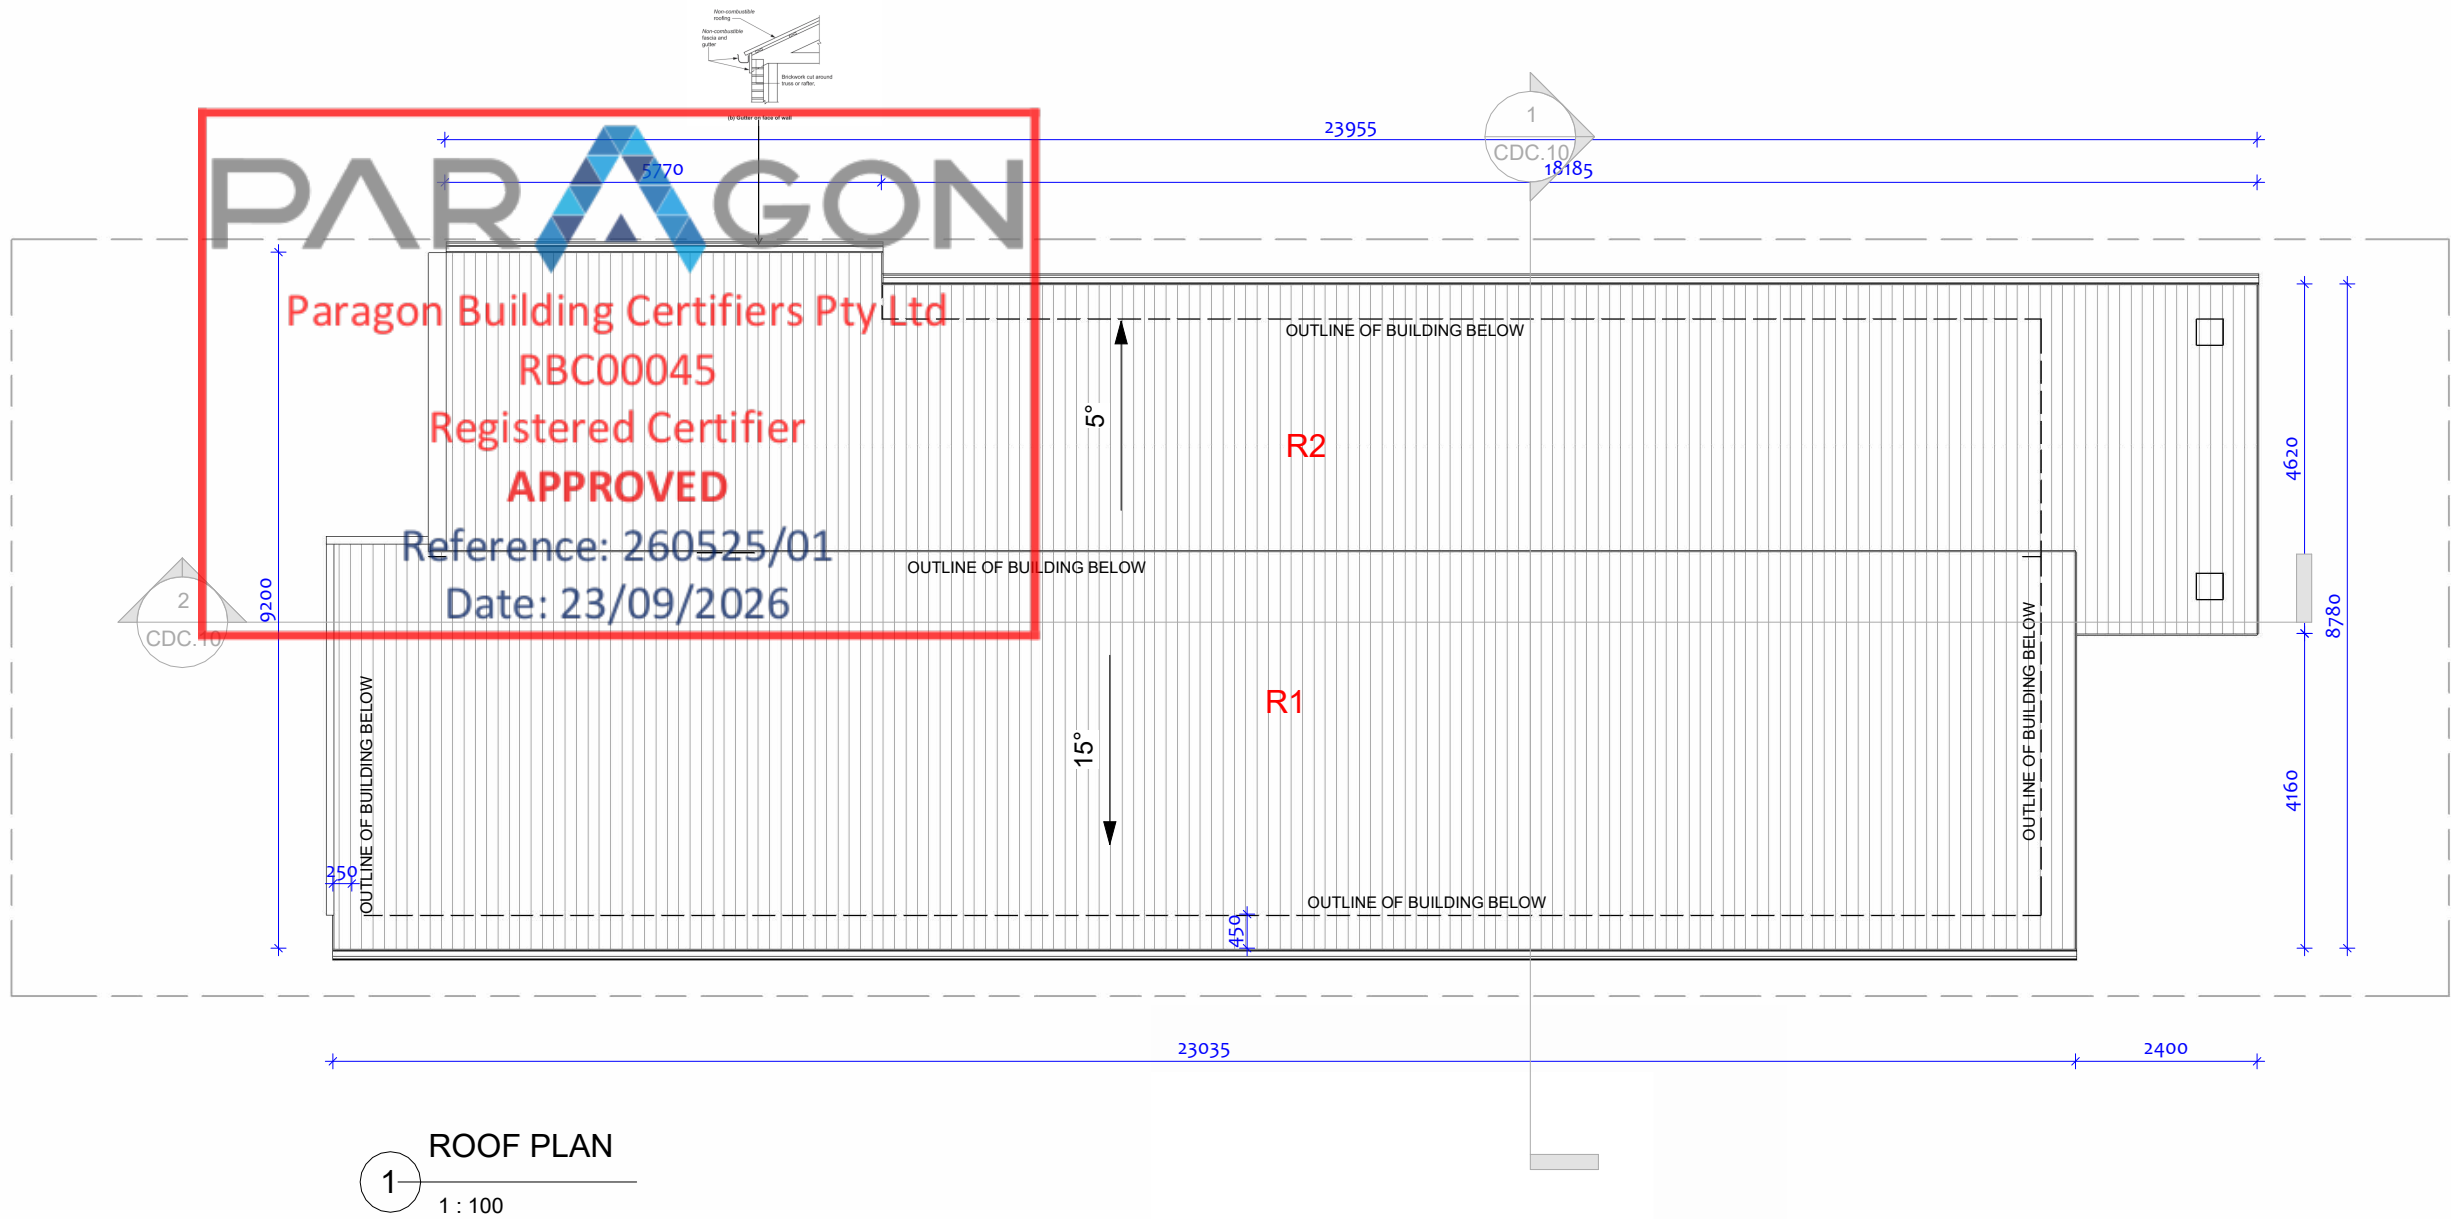

ABCB HOUSING PROVISIONS STANDARD 2022

10.8.3 VENTILATION OF ROOF SPACES

1. IN CLIMATE ZONES 6,7 AND 8, A ROOF MUST HAVE A ROOF SPACE THAT

(A) IS LOCATED

(I) IMMEDIATELY ABOVE THE PRIMARY INSULATION LAYER, OR

(II) IMMEDIATELY ABOVE SARKING WITH A PERMEANCE OF NOT LESS THAN 1.14 µG/N.S, IMMEDIATELY ABOVE THE PRIMARY INSULATION LAYER, OR

(III) IMMEDIATELY ABOVE CEILING INSULATION MEETS THE REQUIREMENTS OF 13.2.3(3) AND 13.2.3(4); AND



(B) HAS A HEIGHT OF NOT LESS THAN 20MM; AND

(C) IS EITHER -

(I) VENTILATED TO OUTDOOR AIR THROUGH DISTRIBUTED OPENINGS IN ACCORDANCE WITH TABLE 10.8.3; OR


(II) LOCATED IMMEDIATELY UNDERNEATH THE TILES OF A UNSARKED TILED ROOF.

Table 10.8.3: Roof space ventilation requirements	
Roof pitch	Ventilation openings
< 10°	25,000 mm ² /m provided at each of two opposing ends
≥ 10° and < 15°	25,000 mm ² /m provided at the eaves and 5,000 mm ² /m at high level
≥ 15° and < 75°	7,000 mm ² /m provided at the eaves and 5,000 mm ² /m at high level, plus an additional 18,000 mm ² /m at the eaves if the roof has a cathedral ceiling

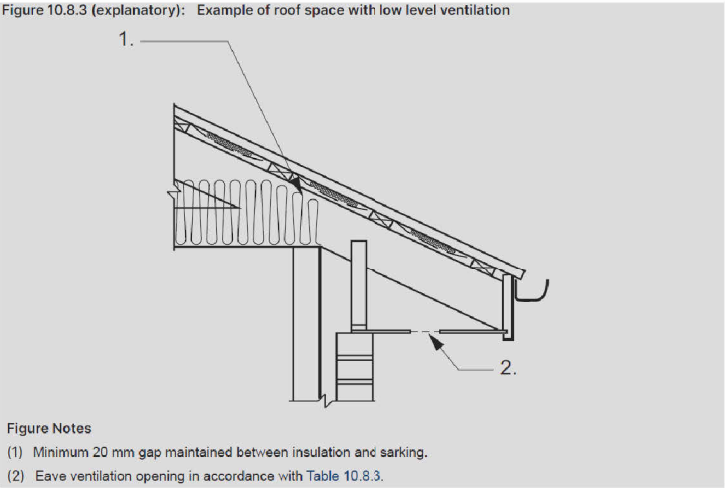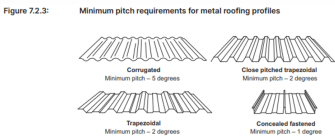

Roof Schedule			
Mark	Base Level	Area	Comments
R1	Level 1	125 m ²	COLORBOND (Black Or shades of grey Or Neutral color)
R2	Level 1	92 m ²	COLORBOND (Black Or shades of grey Or Neutral color)
Grand total: 2		217 m ²	


REV	DATE	DESCRIPTION	BY
8	17-09-2026	Roof Updated	
7	28-08-2026	CDC ISSUE	
5	30-06-2026	Bar Fridge added and raked ceiling to lounge, hallway & living room-Ekta	

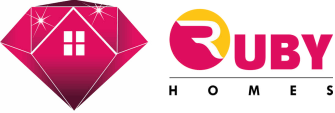


THIS DRAWING IS THE EXCLUSIVE PROPERTY OF THE DEVELOPER & THE REPRODUCTION OF ANY PART WITHOUT THE PRIOR WRITTEN CONSENT OF THE DEVELOPER IS A VIOLATION OF APPLICABLE LAWS. IN NO EVENT SHALL THE DEVELOPER BE HELD LIABLE FOR SPECIAL COLLATERAL, INCIDENTAL OR CONSEQUENTIAL LIABILITY IN CONNECTION WITH THE USE OF THIS DIGITAL DATA ONCE RELEASED FROM THE DEVELOPER'S OFFICE. THIS DRAWING IS TO BE READ & UNDERSTOOD IN CONJUNCTION WITH THE STRUCTURAL, MECHANICAL, ELECTRICAL & / OR ANY OTHER CONSULTANT'S DOCUMENTATION AS MAY BE APPLICABLE TO THE PROJECT PRIOR TO THE START OF ANY WORKS AND FOR ITS DURATION.

PROJECT:
LOT 644 WURRIDJAL STREET
LOT 644 4 WURRIDJAL STREET
AUSTRAL 2179

DRAWING TITLE:
ROOF PLAN

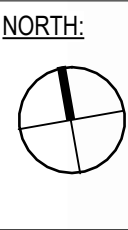

LOT NO:	DATE:	SCALE:	<u>DRAWING</u> No:	<u>REV:</u>
644	18-09-2026	1 : 100	CDC.07	8
DRAWN BY:	CHECKED BY:			ISSUED BY:
AS	RH			
DRAFTED BY:	CLIENT NAME:			
RS	Anish KC and Deepa Basnet			

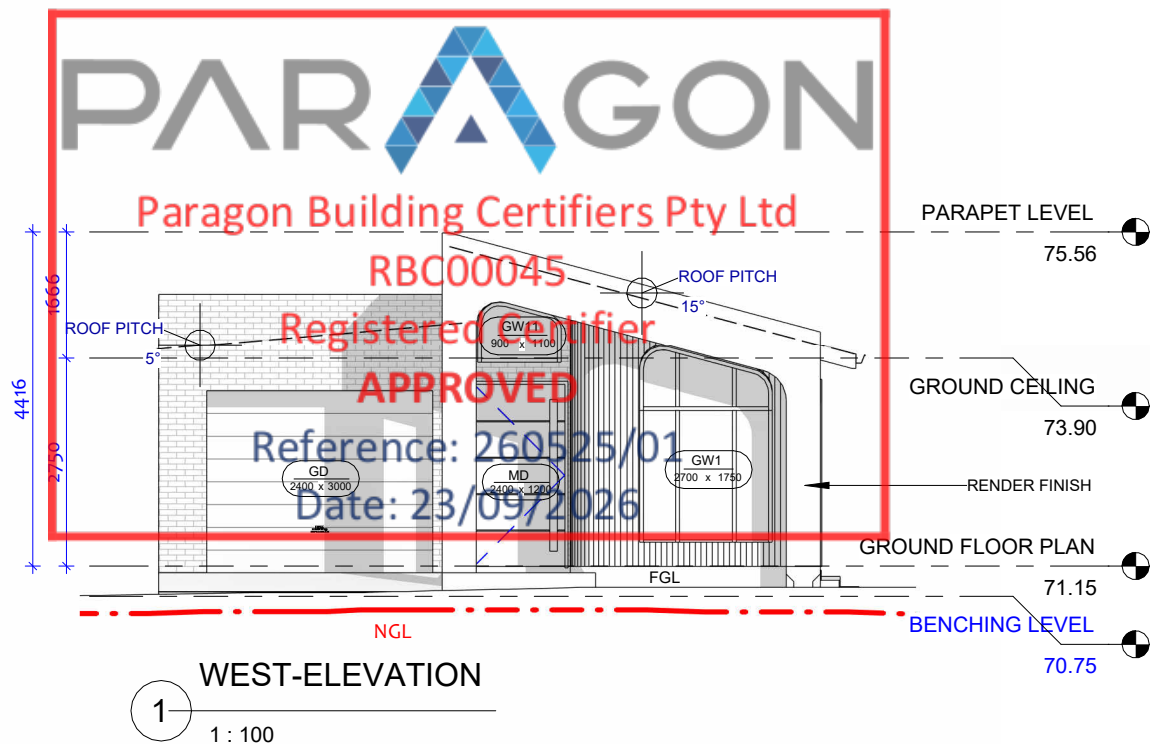

Window Schedule 1					
Mark	Height	Width	Sill Height	Head Height	Description

GROUND FLOOR PLAN


GW1	2700	1750	320	3020	FIXED
GW2	1400	1500	1000	2400	SLIDING
GW3	1400	1500	1000	2400	SLIDING
GW4	600	2200	950	1550	FIXED
GW5	2000	1800	400	2400	SLIDING
GW6	1400	2000	1000	2400	SLIDING
GW7	1400	1500	1000	2400	SLIDING
GW8	500	1200	1900	2400	SLIDING
GW9	1400	1800	1000	2400	SLIDING
GW10	600	800	1800	2400	SLIDING
GW11	900	1100	2692	3592	FIXED

GROUND FLOOR PLAN: 11

Level 1

RW1	400	2500	350	750	FIXED
RW2	400	2500	350	750	FIXED
RW3	400	2500	350	750	FIXED

Level 1: 3

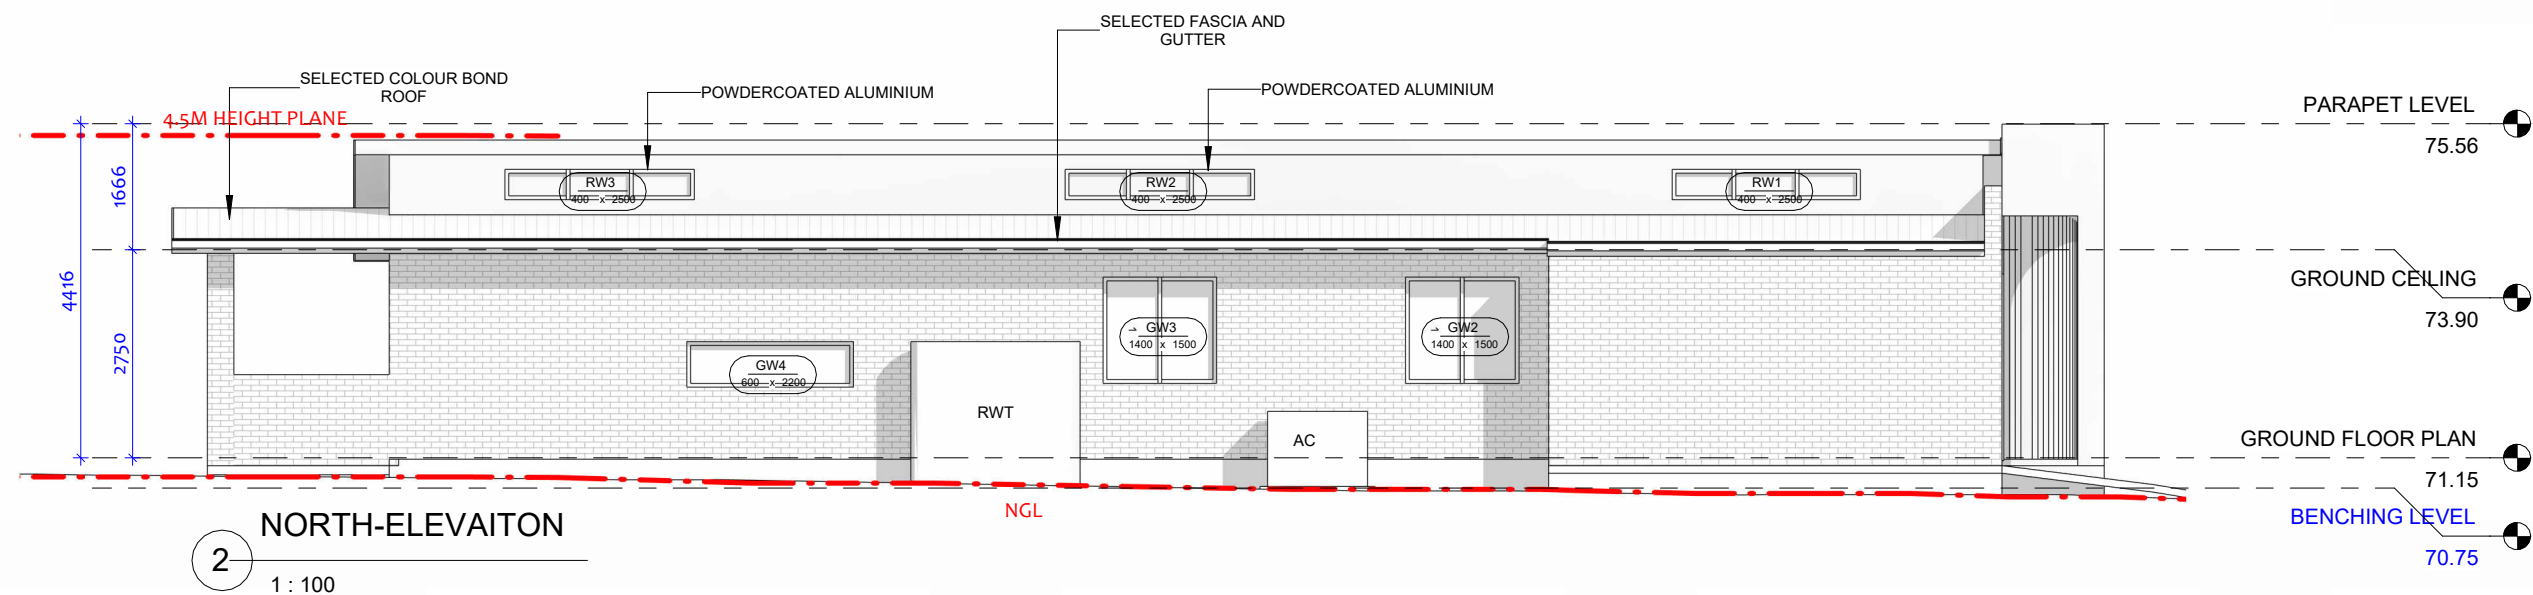

REV	DATE	DESCRIPTION	BY
8	17-09-2026	Roof Updated	
7	28-08-2026	CDC ISSUE	
6	2-07-2026	Front windows curved - Sudeep	
4	29-06-2026	GW1 angled window - Ekta	
3	26-06-2026	Facade Updated with PVC panels - Ekta	
2	23-04-2026	Curved wall on facade and WIR, Bed2 reduce by 200mm to give space for dining, Puja nook added from WIP space - Client Meeting	

RUBY HOMES

THIS DRAWING IS THE EXCLUSIVE PROPERTY OF THE DEVELOPER & THE REPRODUCTION OF ANY PART WITHOUT THE PRIOR WRITTEN CONSENT OF THE DEVELOPER IS A VIOLATION OF APPLICABLE LAWS. IN NO EVENT SHALL THE DEVELOPER BE HELD LIABLE FOR SPECIAL COLLATERAL, INCIDENTAL OR CONSEQUENTIAL LIABILITY IN CONNECTION WITH THE USE OF THIS DIGITAL DATA ONCE RELEASED FROM THE DEVELOPER'S OFFICE. THIS DRAWING IS TO BE READ & UNDERSTOOD IN CONJUNCTION WITH THE STRUCTURAL, MECHANICAL, ELECTRICAL & / OR ANY OTHER CONSULTANT'S DOCUMENTATION AS MAY BE APPLICABLE TO THE PROJECT PRIOR TO THE START OF ANY WORKS AND FOR ITS DURATION.

PROJECT:
LOT 644 WURRIDJAL STREET
LOT 644 4 WURRIDJAL STREET
AUSTRAL 2179

DRAWING TITLE:
ELEVATION 01

NORTH:

LOT NO:	DATE:	SCALE:	DRAWING No:	REV:
644	18-09-2026	1 : 100	CDC.08	8
DRAWN BY:	CHECKED BY:	DRAFTED BY:	CLIENT NAME:	ISSUED BY:
AS	RH	RS	Anish KC and Deepa Basnet	

CDC ISSUE




Door Schedule 1				
Mark	Height	Width	Count	Description

GROUND FLOOR PLAN

D1	2340	820	1	FLUSH DOOR
D2	2340	820	1	FLUSH DOOR
D3	2340	720	1	FLUSH DOOR
D4	2340	820	1	FLUSH DOOR
D5	2340	820	1	FLUSH DOOR
D6	2340	720	1	FLUSH DOOR
D7	2340	720	1	FLUSH DOOR
D8	2340	720	1	FLUSH DOOR
D9	2340	820	1	FLUSH DOOR
GD	2400	3000	1	GARAGE DOOR
MD	2400	1200	1	SOLID CORE DOOR
SD1	2300	2100	1	

GROUND FLOOR PLAN: 12

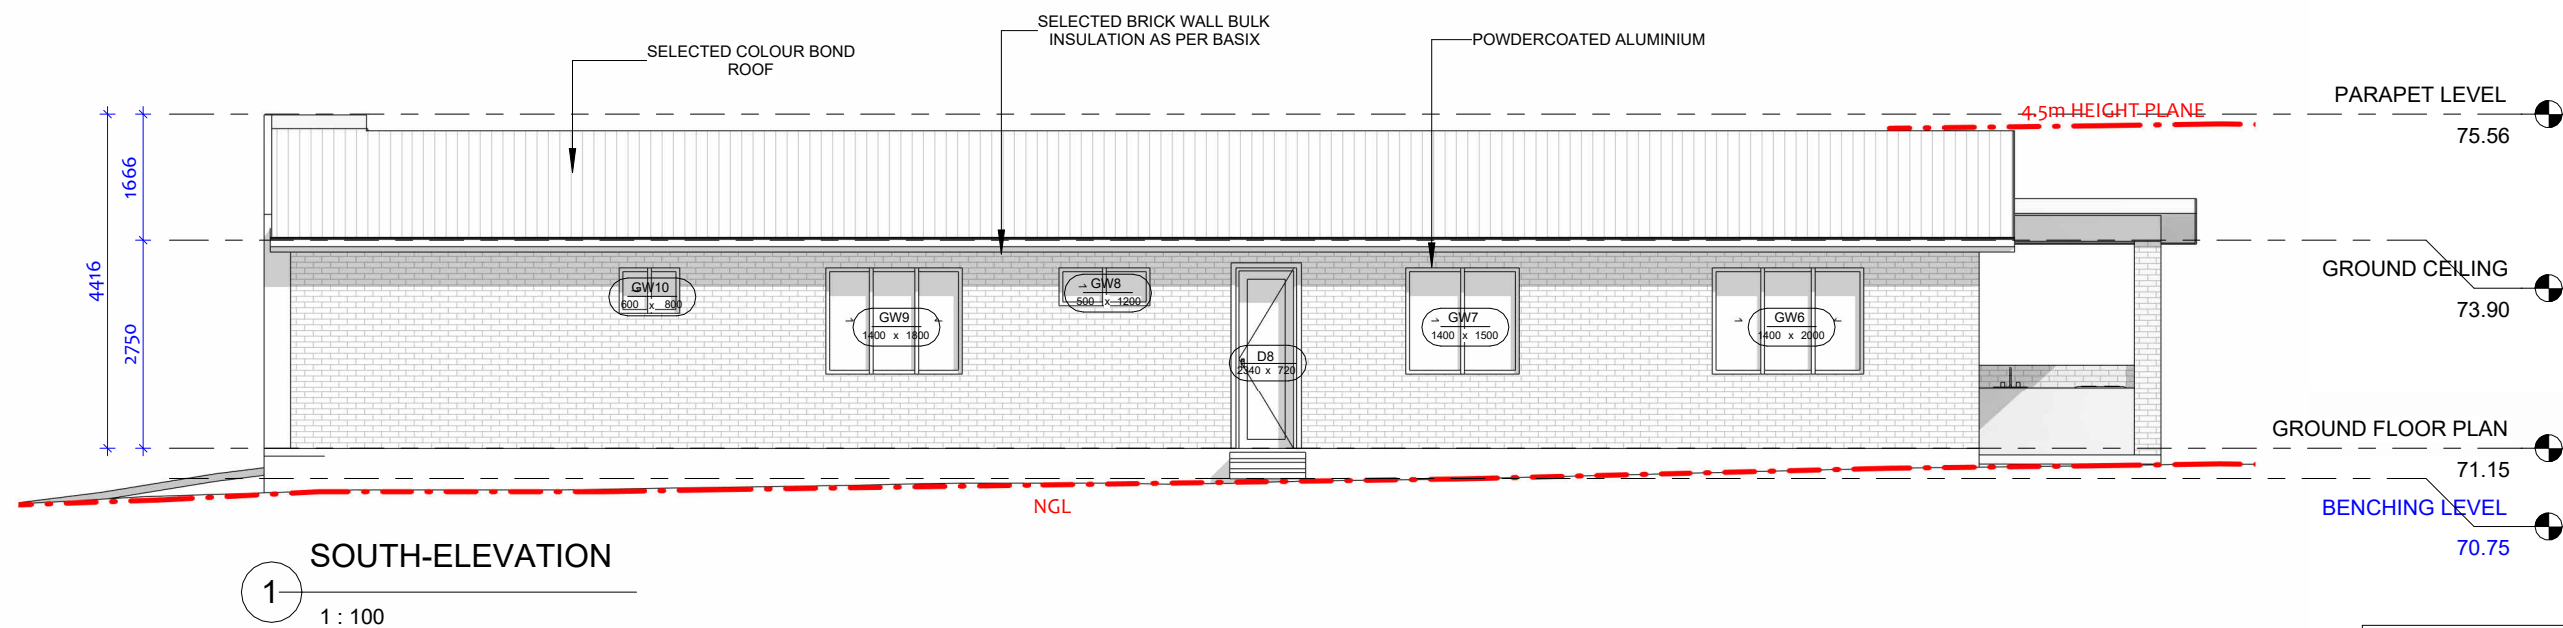

REV	DATE	DESCRIPTION	BY
8	17-09-2026	Roof Updated	
7	28-08-2026	CDC ISSUE	



RUBY
HOMES

THIS DRAWING IS THE EXCLUSIVE PROPERTY OF THE DEVELOPER & THE REPRODUCTION OF ANY PART WITHOUT THE PRIOR WRITTEN CONSENT OF THE DEVELOPER IS A VIOLATION OF APPLICABLE LAWS. IN NO EVENT SHALL THE DEVELOPER BE HELD LIABLE FOR SPECIAL COLLATERAL, INCIDENTAL OR CONSEQUENTIAL LIABILITY IN CONNECTION WITH THE USE OF THIS DIGITAL DATA ONCE RELEASED FROM THE DEVELOPER'S OFFICE. THIS DRAWING IS TO BE READ & UNDERSTOOD IN CONJUNCTION WITH THE STRUCTURAL, MECHANICAL, ELECTRICAL & / OR ANY OTHER CONSULTANT'S DOCUMENTATION AS MAY BE APPLICABLE TO THE PROJECT PRIOR TO THE START OF ANY WORKS AND FOR ITS DURATION.

PROJECT:
LOT 644 WURRIDJAL STREET
LOT 644 4 WURRIDJAL STREET
AUSTRAL 2179

DRAWING TITLE:
ELEVATION 02

NORTH:

LOT NO:	DATE:	SCALE:	DRAWING No:	REV:
644	18-09-2026	1 : 100	CDC.09	8
DRAWN BY:	CHECKED BY:			ISSUED BY:
AS	RH			
DRAFTED BY:	CLIENT NAME:			
RS	Anish KC and Deepa Basnet			

CDC ISSUE

PARAGON

Paragon Building Certifiers Pty Ltd


RBC00045

Registered Certifier

APPROVED

Reference: 260525/01


Date: 23/09/2026

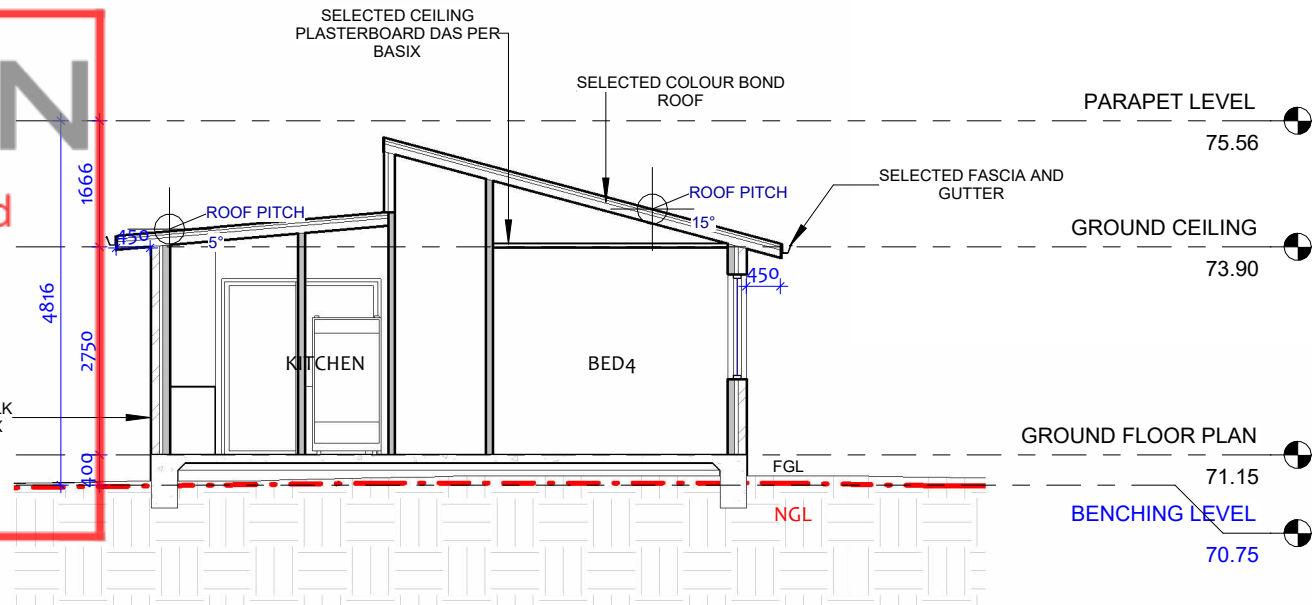

CROSS SECTION

1

1 : 100

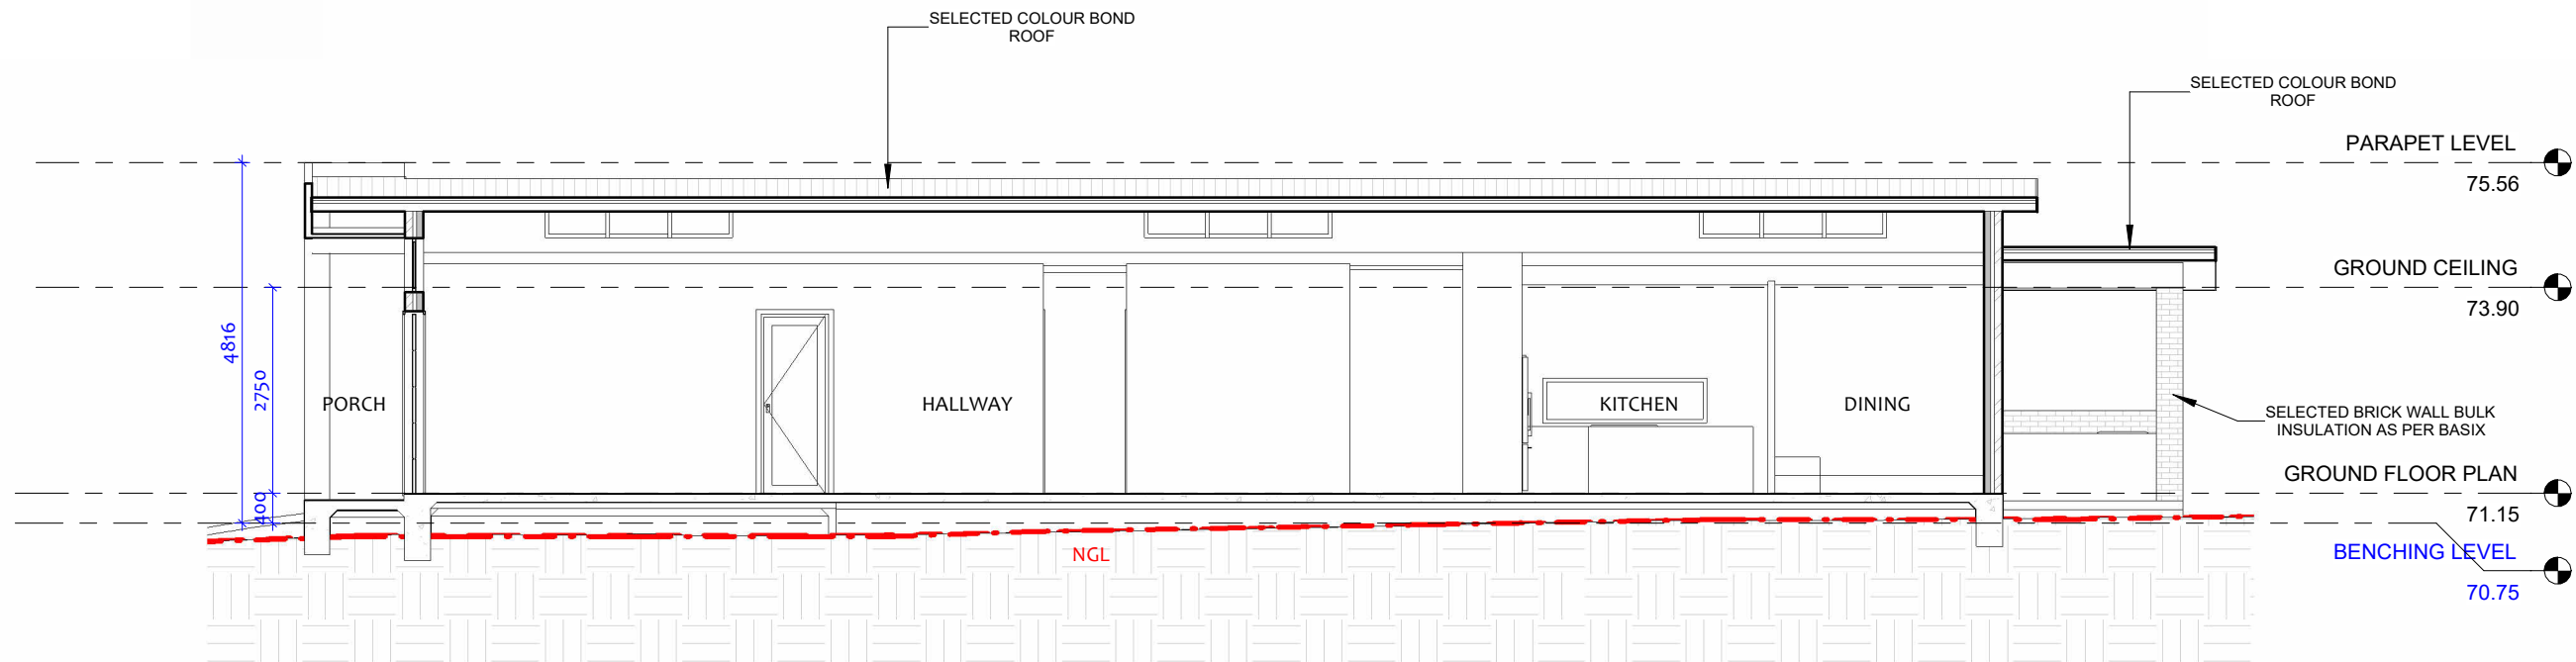

LONGITUDINAL SECTION

2

1 : 100

				CDC ISSUE								
				 THIS DRAWING IS THE EXCLUSIVE PROPERTY OF THE DEVELOPER & THE REPRODUCTION OF ANY PART WITHOUT THE PRIOR WRITTEN CONSENT OF THE DEVELOPER IS A VIOLATION OF APPLICABLE LAWS. IN NO EVENT SHALL THE DEVELOPER BE HELD LIABLE FOR SPECIAL COLLATERAL, INCIDENTAL OR CONSEQUENTIAL LIABILITY IN CONNECTION WITH THE USE OF THIS DIGITAL DATA ONCE RELEASED FROM THE DEVELOPER'S OFFICE. THIS DRAWING IS TO BE READ & UNDERSTOOD IN CONJUNCTION WITH THE STRUCTURAL, MECHANICAL, ELECTRICAL & / OR ANY OTHER CONSULTANT'S DOCUMENTATION AS MAY BE APPLICABLE TO THE PROJECT PRIOR TO THE START OF ANY WORKS AND FOR ITS DURATION.	PROJECT: LOT 644 WURRIDJAL STREET LOT 644 4 WURRIDJAL STREET AUSTRAL 2179	DRAWING TITLE: SECTIONS	NORTH:	LOT NO:	DATE:	SCALE: 1 : 100	DRAWING No:	REV:
644	18-09-2026		7									
DRAWN BY:	CHECKED BY:	CDC.10	ISSUED BY:									
AS	RH											
DRAFTED BY:	CLIENT NAME:											
RS	Anish KC and Deepa Basnet											
7	28-08-2026	CDC ISSUE										
REV	DATE	DESCRIPTION	BY									

THIS DRAWING IS THE EXCLUSIVE PROPERTY OF THE DEVELOPER & THE REPRODUCTION OF ANY PART WITHOUT THE PRIOR WRITTEN CONSENT OF THE DEVELOPER IS A VIOLATION OF APPLICABLE LAWS. IN NO EVENT SHALL THE DEVELOPER BE HELD LIABLE FOR SPECIAL COLLATERAL, INCIDENTAL OR CONSEQUENTIAL LIABILITY IN CONNECTION WITH THE USE OF THIS DIGITAL DATA ONCE RELEASED FROM THE DEVELOPER'S OFFICE. THIS DRAWING IS TO BE READ & UNDERSTOOD IN CONJUNCTION WITH THE STRUCTURAL, MECHANICAL, ELECTRICAL & / OR ANY OTHER CONSULTANT'S DOCUMENTATION AS MAY BE APPLICABLE TO THE PROJECT PRIOR TO THE START OF ANY WORKS AND FOR ITS DURATION.

PARAGON

Paragon Building Certifiers Pty Ltd


RBC00045

Registered Certifier

APPROVED

Reference: 260525/01

Date: 23/09/2026

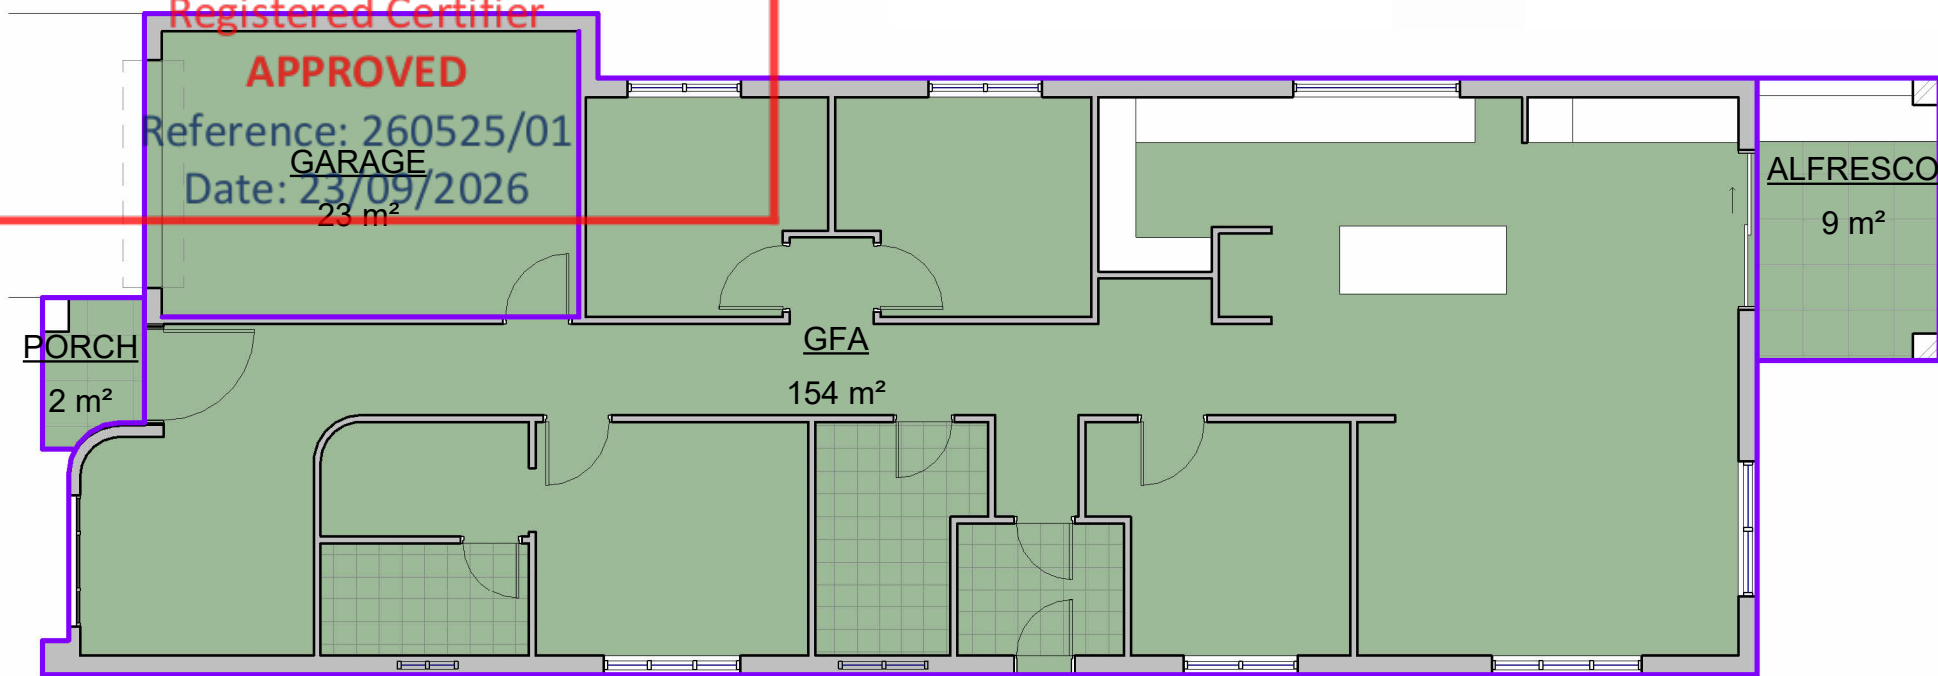

1 GROUND FLOOR PLAN
1 : 100

Area Schedule (Gross Building)	
Name	Area

GROUND FLOOR PLAN	
GFA	154 m²
PORCH	2 m²
ALFRESCO	9 m²
GARAGE	23 m²
GROUND FLOOR PLAN: 4	188 m²
Grand total: 4	188 m²

				CDC ISSUE								
				 THIS DRAWING IS THE EXCLUSIVE PROPERTY OF THE DEVELOPER & THE REPRODUCTION OF ANY PART WITHOUT THE PRIOR WRITTEN CONSENT OF THE DEVELOPER IS A VIOLATION OF APPLICABLE LAWS. IN NO EVENT SHALL THE DEVELOPER BE HELD LIABLE FOR SPECIAL COLLATERAL, INCIDENTAL OR CONSEQUENTIAL LIABILITY IN CONNECTION WITH THE USE OF THIS DIGITAL DATA ONCE RELEASED FROM THE DEVELOPER'S OFFICE. THIS DRAWING IS TO BE READ & UNDERSTOOD IN CONJUNCTION WITH THE STRUCTURAL, MECHANICAL, ELECTRICAL & / OR ANY OTHER CONSULTANT'S DOCUMENTATION AS MAY BE APPLICABLE TO THE PROJECT PRIOR TO THE START OF ANY WORKS AND FOR ITS DURATION.	PROJECT:	DRAWING TITLE:	NORTH:	LOT NO:	DATE:	SCALE:	DRAWING No:	REV:
					LOT 644 WURRIDJAL STREET	FLOOR AREA PLAN		644	18-09-2026	1 : 100	CDC.11	7
7	28-08-2026	CDC ISSUE			LOT 644 4 WURRIDJAL STREET AUSTRAL 2179			DRAWN BY:	CHECKED BY:			ISSUED BY:
2	23-04-2026	Curved wall on facade and WIR, Bed2 reduce by 200mm to give space for dining, Puja nook added from WIP space - Client Meeting						AS	RH			
1	09-04-2026	Concept Issue										
REV	DATE	DESCRIPTION	BY					DRAFTED BY:	CLIENT NAME:			
							RS	Anish KC and Deepa Basnet				



Paragon Building Certifiers Pty Ltd


RBC00045

Registered Certifier

APPROVED

Reference: 260525/01

Date: 23/09/2026

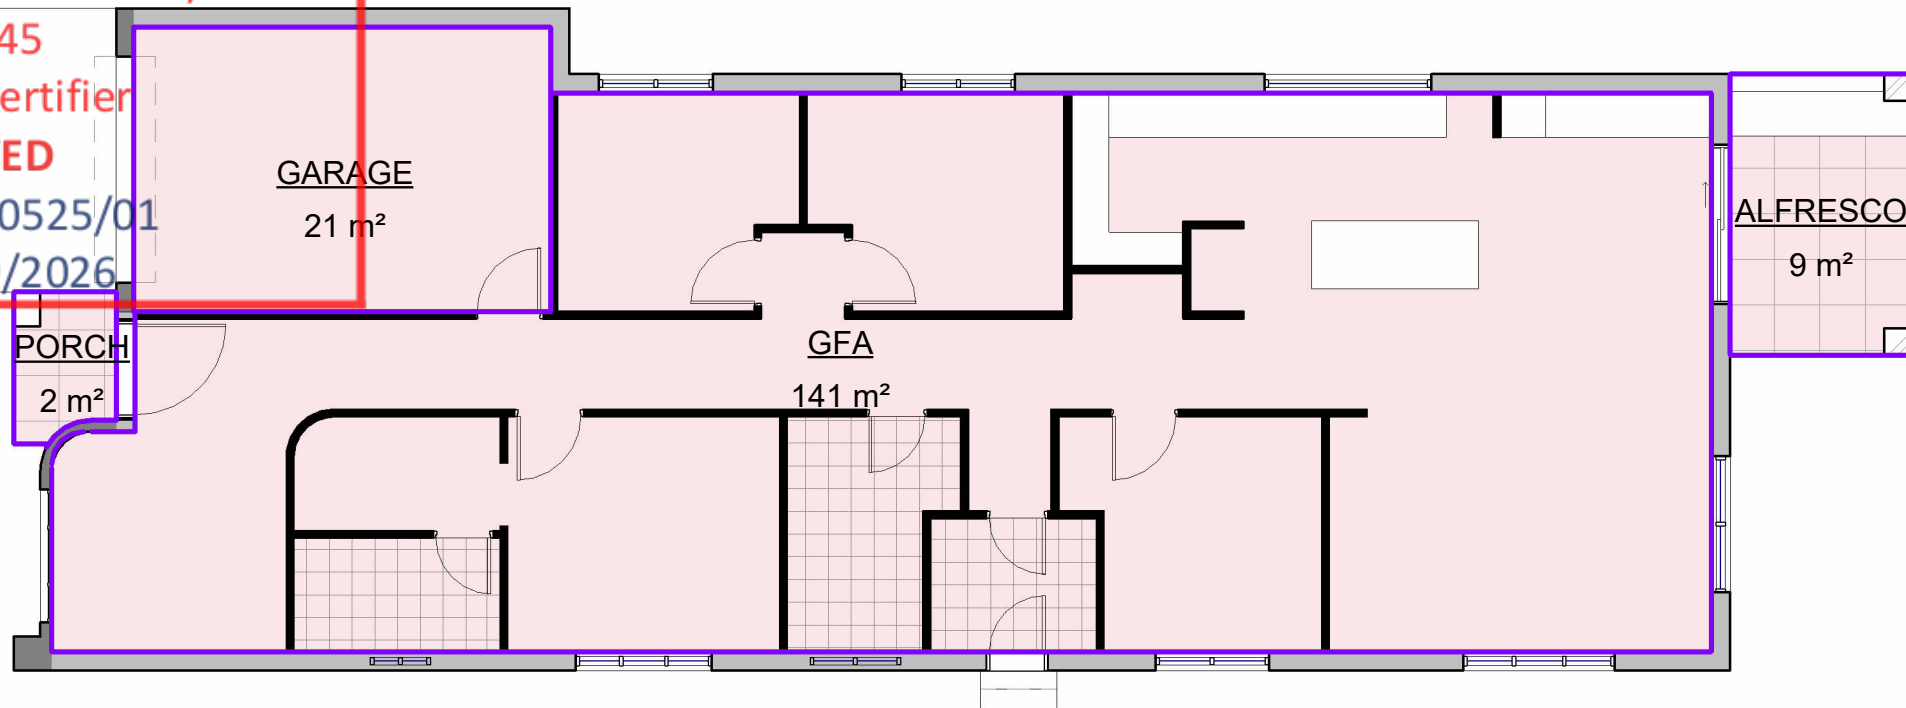

GROUND FLOOR PLAN

1

1 : 100

Area Schedule (Rentable)

Name

Area

GROUND FLOOR PLAN

PORCH	2 m ²
GARAGE	21 m ²
GFA	141 m ²
ALFRESCO	9 m ²
GROUND FLOOR PLAN: 4	173 m ²
Grand total: 4	173 m ²

CDC ISSUE

7	28-08-2026	CDC ISSUE	
REV	DATE	DESCRIPTION	BY



THIS DRAWING IS THE EXCLUSIVE PROPERTY OF THE DEVELOPER & THE REPRODUCTION OF ANY PART WITHOUT THE PRIOR WRITTEN CONSENT OF THE DEVELOPER IS A VIOLATION OF APPLICABLE LAWS. IN NO EVENT SHALL THE DEVELOPER BE HELD LIABLE FOR SPECIAL COLLATERAL, INCIDENTAL OR CONSEQUENTIAL LIABILITY IN CONNECTION WITH THE USE OF THIS DIGITAL DATA ONCE RELEASED FROM THE DEVELOPER'S OFFICE. THIS DRAWING IS TO BE READ & UNDERSTOOD IN CONJUNCTION WITH THE STRUCTURAL, MECHANICAL, ELECTRICAL & / OR ANY OTHER CONSULTANT'S DOCUMENTATION AS MAY BE APPLICABLE TO THE PROJECT PRIOR TO THE START OF ANY WORKS AND FOR ITS DURATION.

PROJECT:

LOT 644 WURRIDJAL STREET

LOT 644 4 WURRIDJAL STREET

AUSTRAL 2179

DRAWING TITLE:

RENTABLE AREA PLAN

NORTH:



LOT NO:	644	DATE:	18-09-2026	SCALE:	1 : 100	DRAWING No:	CDC.12	REV:	7
DRAWN BY:	AS	CHECKED BY:	RH					ISSUED BY:	
DRAFTED BY:	RS	CLIENT NAME:							Anish KC and Deepa Basnet

PARAGON

Paragon Building Certifiers Pty Ltd


RBC00045

Registered Certifier

APPROVED

Reference: 260525/Q1

Date: 23/09/2026

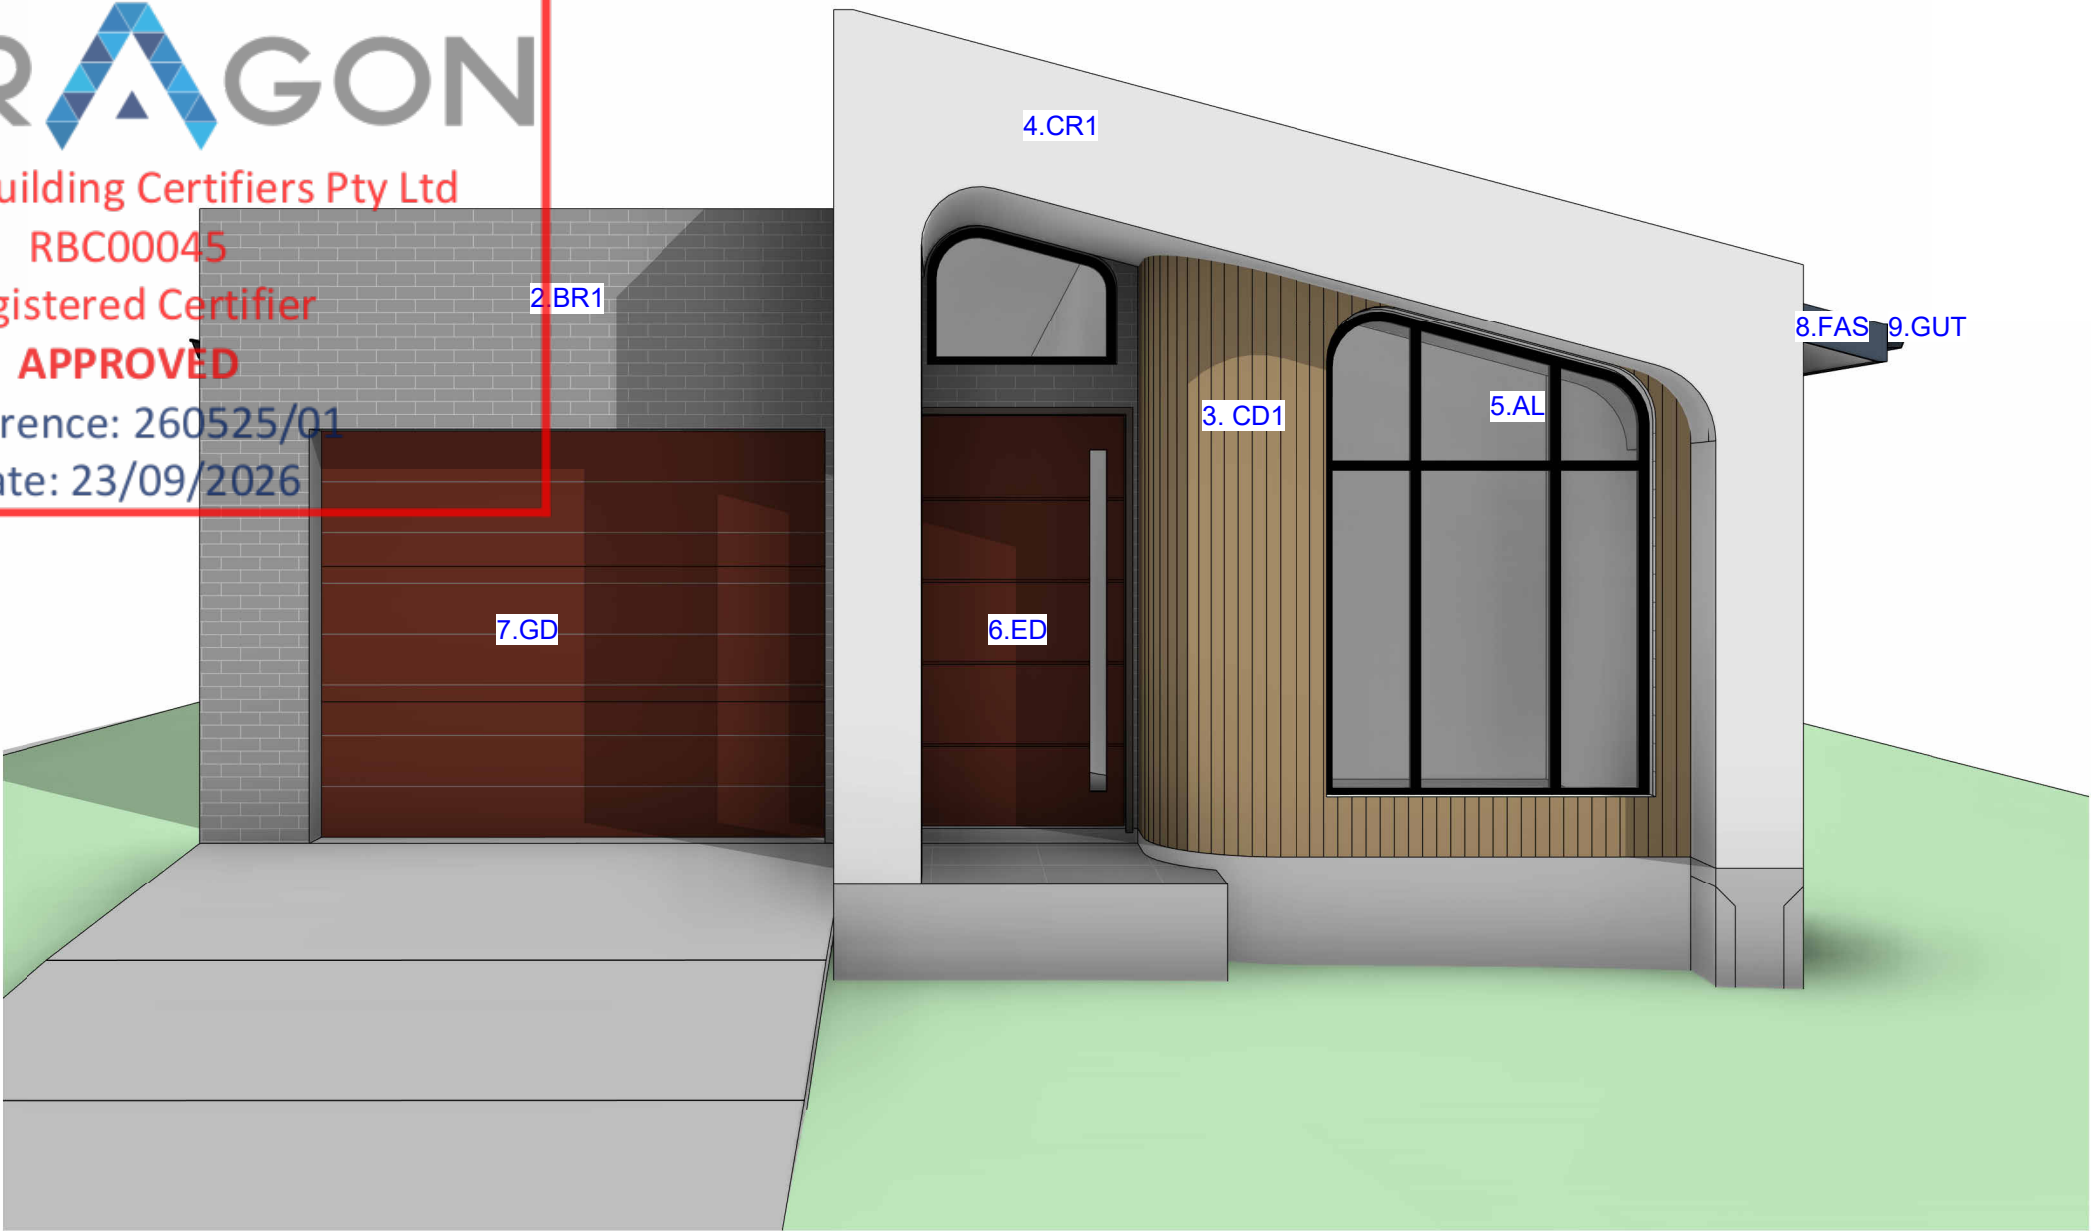

	1. RF	2. BR1	3. CD1	4. CR1	5. AL	6. ED	7. GD	8. FAS	9. GUT
	ROOF	MAIN WALLS	CLADDING	ACCENT 1/RENDER	WINDOWS/ BALUSTRADE	MAIN DOOR	GARAGE DOOR	FASCIA	GUTTER
MATERIAL	COLORBOND DARK MONUMENT	BRICK	BLUEBOARD	BRICK	ALUMINIUM	TIMBER	COLORBOND	COLORBOND	COLORBOND
COLOUR									

NOTE : ALL COLOURS SPECIFIED ARE INDICATIVE ONLY AND ARE SUBJECT TO VARIATION AND TO AVAILABILITY
ANY DISCREPANCY PLEASE FOLLOW AS PER RENDERED IMAGE

REV	DATE	DESCRIPTION	BY
7	28-08-2026	CDC ISSUE	

THIS DRAWING IS THE EXCLUSIVE PROPERTY OF THE DEVELOPER & THE REPRODUCTION OF ANY PART WITHOUT THE PRIOR WRITTEN CONSENT OF THE DEVELOPER IS A VIOLATION OF APPLICABLE LAWS. IN NO EVENT SHALL THE DEVELOPER BE HELD LIABLE FOR SPECIAL COLLATERAL, INCIDENTAL OR CONSEQUENTIAL LIABILITY IN CONNECTION WITH THE USE OF THIS DIGITAL DATA ONCE RELEASED FROM THE DEVELOPER'S OFFICE. THIS DRAWING IS TO BE READ & UNDERSTOOD IN CONJUNCTION WITH THE STRUCTURAL, MECHANICAL, ELECTRICAL & / OR ANY OTHER CONSULTANT'S DOCUMENTATION AS MAY BE APPLICABLE TO THE PROJECT PRIOR TO THE START OF ANY WORKS AND FOR ITS DURATION.


PROJECT:
LOT 644 WURRIDJAL STREET
LOT 644 4 WURRIDJAL STREET
AUSTRAL 2179

DRAWING TITLE:
COLOR SCHEDULE

NORTH:

LOT NO:	DATE:	SCALE:	DRAWING No:	REV:
644	18-09-2026	1 : 100	CDC.14	7
DRAWN BY:	CHECKED BY:	ISSUED BY:		
AS	RH			
DRAFTED BY:	CLIENT NAME:			
RS	Anish KC and Deepa Basnet			

CDC ISSUE

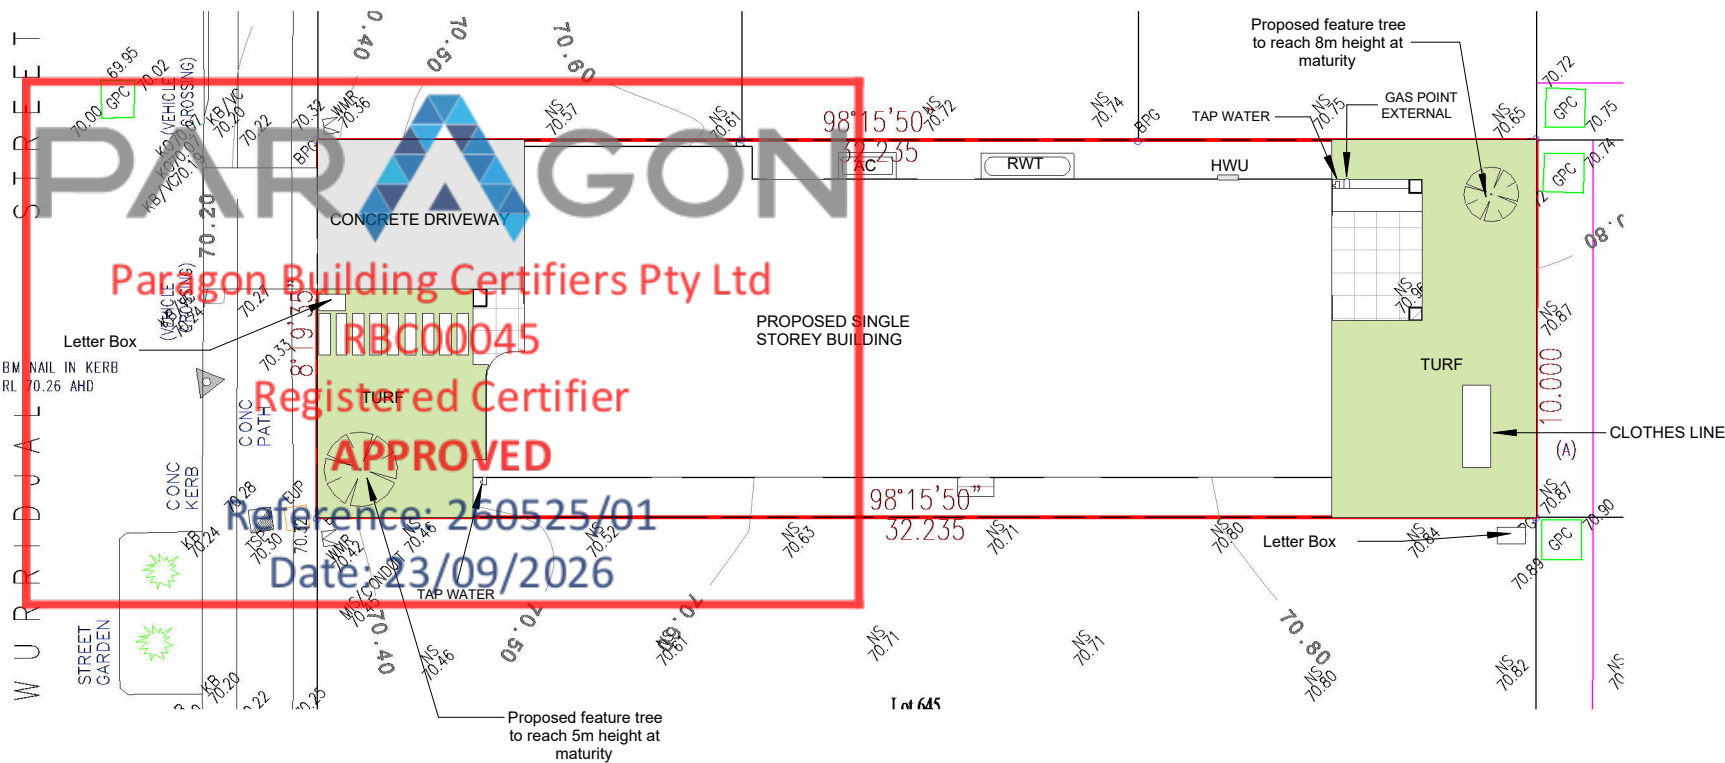

REAR LANDSCAPE AREA = 45.12m²
FRONT LANDSCAPE AREA = 25.9m²
TOTAL LANDSCAPE AREA = 71.02m²

CDC - LANDSCAPE PLAN

1
1 : 200


GENERAL NOTES:

- LANDSCAPE CONTRACTOR TO CHECK DA CONDITIONS AND STAMPED LANDSCAPE PLAN BEFORE COMMENCING WORKS TO ENSURE NO ADDITIONS/AMENDMENTS TO PLAN.
- GARDEN BEDS IN OSD BASIN TO CONSIST OF NON FLOATABLE DECORATIVE GRAVEL.
- REFER TO HYDRAULICS ENGINEERS PLAN FOR OSD DETAILS/FINAL LEVELS.
- MULCHED PLANTING BEDS TO BE A MINIMUM DEPTH OF 75mm AS SELECTED.
- CONTRACTOR'S RESPONSIBILITY TO CHECK AND ADJUST SOIL pH AS REQUIRED.
- PROVIDE TIMBER EDGE AS A MINIMUM BENEATH FENCING/GATES TO DEFINE TURF AND GARDEN BEDS/PATHWAYS, EDGING TO BE PROVIDED TO ALL AREAS WHERE DIFFERING MATERIALS MEET i.e. TURF/GARDEN, TURF/GRAVEL PATH ETC.
- WEED MAT BENEATH GRAVEL GRAVEL PATHWAYS REQUIRED TO LIMIT MUD TRACKING.
- PREMIUM ORGANIC GARDEN MIX TO BE USED.
- ALL PLANTS TO BE HEALTHY AND VIGOROUS.
- CONTRACTOR TO MAKE GOOD TURF ON NATURE STRIP POST CONSTRUCTION.
- CONTRACTOR TO MAKE GOOD TURF ON NATURE STRIP POST CONSTRUCTION.
- DO NOT SCALE ARCHITECTURAL SETOUT FROM LANDSCAPE DRAWING.
- EXISTING TREE SPREAD APPROXIMATE ONLY. REFER TO TREE REPORT WHEN APPLICABLE.
- SITE SURVEY PROVIDED BY OTHERS.
- BUFFALO TURF PREFERRED OVER KIKUYU.

LANDSCAPE BASIX NOTE:
THE APPLICANT MUST PLANT INDIGENEOUS OR LOW WATER USE SPECIES OF VEGETATION THROUGHOUT 15 SQM OF THE SITE.


NOTE : BUILDER RESERVES THE RIGHT NOT TO UNDERTAKE NOR SUPPLY CERTIFICATE FOR OCCUPATION CERTIFICATE.
NOTE : TO AID COMPLIANCE WITH BASIX LEGISLATION, PLANTS (WHERE APPLICABLE) HAVE BEEN SELECTED FROM THE LOCAL CITY COUNCIL/SHIRE PLANT LISTS.
NOTE: LOCATION OF SEWER MAINS/LINES, WATER PIPES, UNDERGROUND ELECTRICITY AND OTHER SERVICES MUST BE OBTAINED PRIOR TO COMMENCEMENT OF ANY WORK ON SITE.

CONTRACTORS NOTE : CALCULATED AREAS DETERMINED BY CAD AND HAVE BEEN ROUNDED UP FOR USE AS A GUIDE ONLY. ALLOW STANDARD PERCENTAGE FOR CUTTING AND WASTAGE. CONFIRM DIMENSIONS AND NUMBERS PRIOR TO QUOTING/ORDERING.

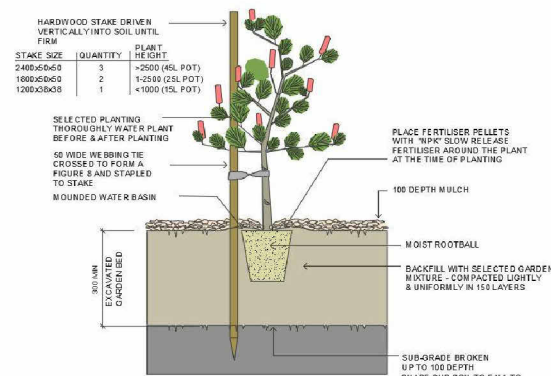

2. TREE & SHRUB PLANTING IN GARDEN BED

NOTE:
DO NOT PLANT IN UNSUITABLE WEATHER CONDITIONS SUCH AS EXTREME HEAT, COLD, WIND OR RAIN.
CLAY SOIL IS TO BE TREATED WITH CLAY BREAKER AND ORGANIC COMPOST.

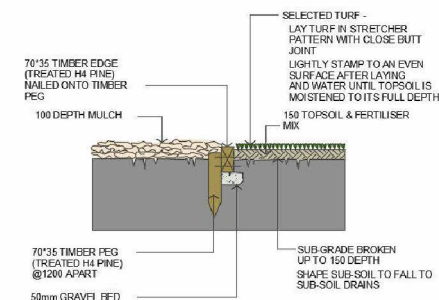

1. TURF & GARDEN EDGE DETAIL

NOTE:
ALIGNMENT OF BRICK EDGE SHALL BE EVEN & FREE FROM DIPS AND HUMPS.

CDC ISSUE

REV	DATE	DESCRIPTION	BY
7	28-08-2026	CDC ISSUE	



THIS DRAWING IS THE EXCLUSIVE PROPERTY OF THE DEVELOPER & THE REPRODUCTION OF ANY PART WITHOUT THE PRIOR WRITTEN CONSENT OF THE DEVELOPER IS A VIOLATION OF APPLICABLE LAWS. IN NO EVENT SHALL THE DEVELOPER BE HELD LIABLE FOR SPECIAL COLLATERAL, INCIDENTAL OR CONSEQUENTIAL LIABILITY IN CONNECTION WITH THE USE OF THIS DIGITAL DATA ONCE RELEASED FROM THE DEVELOPER'S OFFICE. THIS DRAWING IS TO BE READ & UNDERSTOOD IN CONJUNCTION WITH THE STRUCTURAL, MECHANICAL, ELECTRICAL & / OR ANY OTHER CONSULTANT'S DOCUMENTATION AS MAY BE APPLICABLE TO THE PROJECT PRIOR TO THE START OF ANY WORKS AND FOR ITS DURATION.

PROJECT:
LOT 644 WURRIDJAL STREET
LOT 644 4 WURRIDJAL STREET
AUSTRAL 2179

DRAWING TITLE:
LANDSCAPE PLAN



LOT NO:	DATE:	SCALE:	DRAWING No:	REV:
644	18-09-2026	1 : 200	CDC.15	7
DRAWN BY:	CHECKED BY:	CLIENT NAME:	ISSUED BY:	
AS	RH	Anish KC and Deepa Basnet		
DRAFTED BY:	RS			

ABCB HOUSING PROVISIONS : PART 10.2 WET AREA WATERPROOFING

10.2.1 Wet Areas

- 1. Building elements in wet areas within a building must be protected with a waterproofing system.
- 2. The waterproofing system in (1) must be either waterproof or water resistant in accordance with 10.2.2 to 10.2.6.

10.2.2 Shower Area (enclosed and unenclosed)

- 1. For a shower area with a hob, step-down or level threshold, the following applies:
 - a. The floor of the shower area must be waterproof, including any hob or step-down (see Figure 10.2.2); and
 - b. The walls of the shower area must be waterproof not less than 1800 mm above the floor substrate (see Figure 10.2.2).
 - c. Wall junctions and joints within the shower area must be waterproof not less than 40 mm either side of the junction (see Figure 10.2.2).
 - d. Wall/floor junctions within the shower area must be waterproof (see Figure 10.2.2).
 - e. Penetrations within the shower area must be waterproof.
- 2. A shower with a preformed shower base must also comply with the requirements of (1), except for (a) which is not applicable.

Figure 10.2.2: Extent of treatment for shower areas - concrete, compressed fibre-cement and fibre-cement sheet floors.

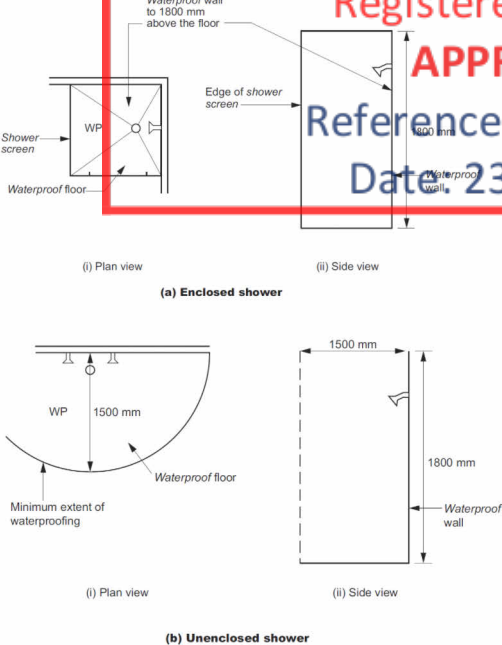


Figure Notes
Wall/floor junction heights are to be as per 10.2.2 to 10.2.6 (as applicable).

Notes
Where a shower is above a bath or spa, use requirements for shower.

10.2.3 Area outside shower area

- 1. For concrete, compressed fibre-cement and fibre-cement sheet flooring, the floor of the room must be water resistant.
- 2. For timber floors including particleboard, plywood and other timber based flooring materials, the floor of the room must be waterproof.
- 3. Wall/floor junctions must be -
 - a. waterproof, and
 - b. where a flashing is used, the horizontal leg must be not less than 40 mm.

10.2.4 Areas adjacent to baths and spas without showers

- 1. For areas adjacent to all baths and spas, the following applies:
 - a. For concrete, compressed fibre-cement and fibre-cement sheet flooring, the floor of the room must be water resistant.
 - b. For timber floors including particleboard, plywood and other timber based flooring materials, the floor of the room must be waterproof.
 - c. Tap and spout penetrations must be waterproof where they occur in horizontal surfaces.
- 2. For areas adjacent to non-freestanding baths and spas, the following applies:
 - a. Walls must be water resistant (see Figure 10.2.4a and Figure 10.2.4b):
 - to a height of not less than 150mm above the vessel, for the extent of the vessel, where the vessel is within 75mm of a wall, and
 - for all exposed surfaces below vessel lip.
 - b. Wall junctions and joints must be water resistant within 150mm above a vessel for the extent of the vessel.
 - c. Wall/floor junctions must be waterproof for the extent of the vessel (see Figure 10.2.4a and Figure 10.2.4b).
- 3. For inserted baths and spas, the following applies:
 - a. For floors and horizontal surfaces:
 - Any shelf area adjoining the bath or spa must be waterproof and include a waterstop under the vessel lip.
 - There are no requirements for the floor under a bath or spa.
 - b. For walls:
 - Waterproof to not less than 150mm above the lip of a bath or spa.
 - There are no requirements for the floor under a bath or spa.
 - c. For wall junctions and joints, the following applies:
 - Waterproof junctions within 150mm of a bath or spa.
 - There are no requirements for junctions and joints in walls beneath the lip of a bath or spa.
 - d. Tap and spout penetrations must be waterproof where they occur in horizontal surfaces.

Figure 10.2.4a: Areas adjacent to baths and spas without showers for concrete, compressed fibre-cement and fibre-cement sheet flooring




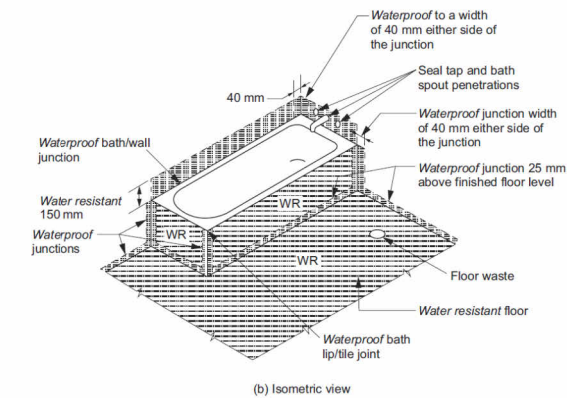



Figure 10.2.4b: Areas adjacent to baths and spas without showers for timber floors including particle-board, plywood and other floor materials

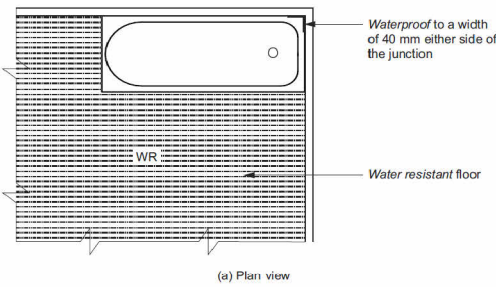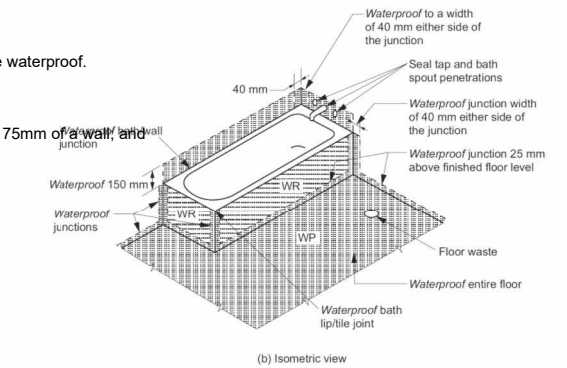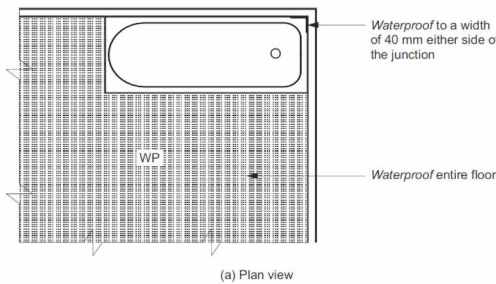

10.2.5 Other areas

- 1. For walls adjoining other types of vessels (e.g. sink, basin or laundry tub), the following applies:
 - a. Walls must be water resistant to a height of not less than 150mm above the vessel, for the extent of the vessel, where the vessel is within 75 mm of a wall (see Figure 10.2.5.)
 - b. Waterproof wall junctions where a vessel is fixed to a wall.
 - c. Waterproof tap and spout penetrations where they occur in surfaces required to be waterproof or water resistant.
- 2. For laundries and WCs, the following applies:
 - a. The floor of the room must be water resistant.
 - b. Wall/floor junctions must be water resistant, and where a flashing is used, the horizontal leg must not be less than 40 mm.
- 3. For WCs with handheld bidet spray installations, the following applies:
 - a. The floor of the room must be waterproof.
 - b. Walls must be -
 - waterproof in WC area within a 900 mm radius from the wall connection of the handheld bidet spray device to a height of not less than 150mm above the floor substrate; and
 - water resistant in WC area within a 900 mm radius from the wall connection of the handheld bidet device to not less than 1200 mm above the finished floor level of the WC.
 - c. Wall junctions within the WC area within 900 mm radius from the wall connection of the handheld bidet spray device must be waterproof.
 - d. Wall/floor junctions within the WC area within 1000 mm radius from the wall connection of the handheld bidet spray device must be waterproof.
 - e. Penetrations in the WC area must be waterproof.

Figure 10.2.5: Bath and vessel abutting wall - areas to be protected

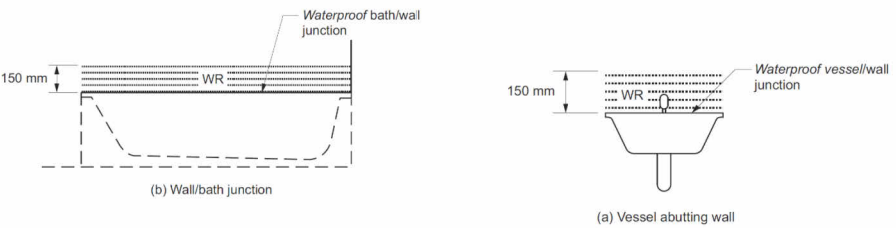

10.2.6 Waterproofing systems

- 1. For the purposes of this Part, a waterproofing system is deemed -
 - a. waterproof, if it complies with (2); or
 - b. water resistant, if it complies with (3).
- 2. For a waterproofing system required to be waterproof in accordance with 10.2.2 to 10.2.5, the materials nominated in 10.2.8 must be used.
- 3. For a waterproofing system required to be water resistant in accordance with 10.2.2 to 10.2.5, the materials nominated in 10.2.9 must be used in conjunction with the materials in 10.2.10.

10.2.12 Construction of wet area floors - falls

- Where a floor waste is installed -
 - a. the minimum continuous fall of a floor plane to the waste must be 1:80; and
 - b. the maximum continuous fall of a floor plane to the waste must be 1:50.

				CDC ISSUE								
				 THIS DRAWING IS THE EXCLUSIVE PROPERTY OF THE DEVELOPER & THE REPRODUCTION OF ANY PART WITHOUT THE PRIOR WRITTEN CONSENT OF THE DEVELOPER IS A VIOLATION OF APPLICABLE LAWS. IN NO EVENT SHALL THE DEVELOPER BE HELD LIABLE FOR SPECIAL COLLATERAL, INCIDENTAL OR CONSEQUENTIAL LIABILITY IN CONNECTION WITH THE USE OF THIS DIGITAL DATA ONCE RELEASED FROM THE DEVELOPER'S OFFICE. THIS DRAWING IS TO BE READ & UNDERSTOOD IN CONJUNCTION WITH THE STRUCTURAL, MECHANICAL, ELECTRICAL & / OR ANY OTHER CONSULTANT'S DOCUMENTATION AS MAY BE APPLICABLE TO THE PROJECT PRIOR TO THE START OF ANY WORKS AND FOR ITS DURATION.	PROJECT: LOT 644 WURRIDJAL STREET LOT 644 4 WURRIDJAL STREET AUSTRAL 2179	DRAWING TITLE: WATERPROOFING DETAILS	NORTH:	LOT NO:	DATE:	SCALE: 1 : 50	DRAWING No:	REV:
7	28-08-2026	CDC ISSUE										
REV	DATE	DESCRIPTION		BY								



THIS DRAWING IS THE EXCLUSIVE PROPERTY OF THE DEVELOPER & THE REPRODUCTION OF ANY PART WITHOUT THE PRIOR WRITTEN CONSENT OF THE DEVELOPER IS A VIOLATION OF APPLICABLE LAWS. IN NO EVENT SHALL THE DEVELOPER BE HELD LIABLE FOR SPECIAL COLLATERAL, INCIDENTAL OR CONSEQUENTIAL LIABILITY IN CONNECTION WITH THE USE OF THIS DIGITAL DATA ONCE RELEASED FROM THE DEVELOPER'S OFFICE. THIS DRAWING IS TO BE READ & UNDERSTOOD IN CONJUNCTION WITH THE STRUCTURAL, MECHANICAL, ELECTRICAL & / OR ANY OTHER CONSULTANT'S DOCUMENTATION AS MAY BE APPLICABLE TO THE PROJECT PRIOR TO THE START OF ANY WORKS AND FOR ITS DURATION.

PROJECT:
LOT 644 WURRIDJAL STREET
LOT 644 4 WURRIDJAL STREET
AUSTRAL 2179

DRAWING TITLE:
WATERPROOFING
DETAILS

NORTH: