

FOR CONSTRUCTION

LOT 27 IN DP 1289262

LOCATED AT NO.7, TRAVELLERS WAY, TAHMOOR NSW 2573.

Proposed Construction of a New Single-Storey Residential Dwelling with Double Garage and Associated Site Works on a Vacant Allotment



OnBuild Certifiers Pty Ltd

Reference: **GENERAL LEGEND**

Date: **06/10/2026**

Andrew Soliman

Director/ Principal Certifier

BB-2940

Consultant who prepared this document

remains responsible for a valid copy

BASIC COMMITMENTS		Certificate number:1859748S
WATER		Date of issue: Thursday, 06 August 2026
LANDSCAPE	230m2	
TOILETS	4 STARS	
KITCHEN TAPS	4 STARS	
SHOWER HEADS	5 STAR (>4.5 but <=6 Umin)	
BASIN TAPS	4 STARS	
ALTERNATIVE WATER	2000L RAINWATER TANK	
ROOF WATER TO TANK	219m2	
ALT.WATER USES- TANK	LAUNDRY	
ALT. WATER USES - RETIC	ALL TOILETS + ONE OUTDOOR TAP	
SWIMMING POOL	N/A	
ENERGY		
HOT WATER	GAS INSTANTANEOUS - 5 STAR	
AIR-CON (HEATING)	3 PHASE DUCTED - EER 3.0-3.5	
AIR-CON (COOLING)	3 PHASE DUCTED - EER 3.0-3.5	
VENTILATION - BATHROOM	VENT INTERLOCKED TO LIGHT	
VENTILATION - KITCHEN	DUCTED - MANUAL SWITCH	
VENTILATION - LAUNDRY	NONE/ NATURAL VENTILATION	
PV SYSTEM	N/A	
COOKTOP	GAS	
OVEN	ELECTRIC	
CLOTHES DRYING	OUTDOOR CLOTHESLINE	
LIGHTING	DEDICATED LED	

CONC.	CONCRETE FLOOR
CPT	CARPET
CRT	CONCRETE ROOF TILES
CR1, CR2 etc.	CEMENT RENDER TYPE/COLOUR
DP/S	DOWN PIPE
DW	DISH WASHER
ED	ENTRY DOOR
F	FRIDGE
FAS	FASCIA
FET	FEATURE TILE
FT, FT1, FT2 etc.	FLOOR TILES
FW	FLOOR WASTE
GD	GARAGE DOOR
GUT	GUTTER
HWU	HOT WATER UNIT
HYB	HYBRID FLOOR
L	LINEN
MR	METAL ROOF
MW	MICROWAVE OVEN
NGL	NATURAL GROUND LEVEL
OBS	OBSCURED GLASS
P	PANTRY
R	ROBE
RL	REDUCED LEVEL
RWH	RAIN WATER HEAD
RWT	RAIN WATER TANK
S	STORAGE
TOW	TOP OF WALL
TL	TIMER LAMINATE
WC	WATER CLOSET
WM	WASHING MACHINE
SD	SMOKE DETECTOR

Sheet List			
Sheet No.	Sheet Name	Issued To	Revision
CC.01	COVER SHEET	CC ISSUE	7
CC.02A	GENERAL NOTES	CC ISSUE	7
CC.02B	GENERAL NOTES	CC ISSUE	7
CC.03	LOCATION PLAN AND SITE PLAN	CC ISSUE	7
CC.04	SITE CUT & FILL PLAN	CC ISSUE	7
CC.05	SITE ANALYSIS AND SEDIMENT CONTROL	CC ISSUE	7
CC.06	GROUND FLOOR PLAN	CC ISSUE	7
CC.07	ROOF PLAN	CC ISSUE	7
CC.08	ELEVATION 01	CC ISSUE	7

Sheet List			
Sheet No.	Sheet Name	Issued To	Revision
CC.09	ELEVATION 02	CC ISSUE	7
CC.10	SECTIONS	CC ISSUE	7
CC.11	FLOOR AREA PLAN	CC ISSUE	7
CC.12	RENTABLE AREA PLAN	CC ISSUE	7
CC.13	BASIX	CC ISSUE	7
CC.14	COLOR SCHEDULE	CC ISSUE	7
CC.15	LANDSCAPE PLAN	CC ISSUE	7
CC.16	DRIVEWAY PLAN	CC ISSUE	7
CC.17	WATERPROOFING DETAILS	CC ISSUE	7

NOTE: ALL IMAGES ARE FOR ILLUSTRATION ONLY AND ARE SUBJECT TO VARIATION AS PER SITE CONDITION, STRUCTURAL ELEMENT AND TO AVAILABILITY OF MATERIALS.

REV	DATE	DESCRIPTION	BY
7	15-09-2026	CC ISSUE	
6	6-08-2026	DA ISSUE	
5	04-06-2026	Window added to Living Room. Highlight window to Bed 3 -Ekta	



THE DRAWING IS THE SOLE PROPERTY OF THE DEVELOPER. THE SIGNATURE OF ANY ARCHITECT OR ENGINEER DOES NOT IMPLY A GUARANTEE OF THE ACCURACY OF ANY INFORMATION OR DATA PROVIDED HEREIN. THE DEVELOPER ACCEPTS NO LIABILITY FOR ANY LOSS OR DAMAGE, INCLUDING CONSEQUENTIAL LOSS OF PROFITS, ARISING FROM THE USE OF THIS DRAWING. THE USER OF THIS DRAWING SHALL BE RESPONSIBLE FOR OBTAINING ALL NECESSARY PERMITS AND APPROVALS FROM THE RELEVANT AUTHORITIES. THE DRAWING IS TO BE USED FOR THE SPECIFIC PROJECT AND SITE ONLY. ANY REUSE OR MODIFICATION OF THIS DRAWING WITHOUT THE WRITTEN CONSENT OF THE DEVELOPER IS STRICTLY PROHIBITED. THE DEVELOPER ACCEPTS NO LIABILITY FOR ANY LOSS OR DAMAGE, INCLUDING CONSEQUENTIAL LOSS OF PROFITS, ARISING FROM THE USE OF THIS DRAWING. THE USER OF THIS DRAWING SHALL BE RESPONSIBLE FOR OBTAINING ALL NECESSARY PERMITS AND APPROVALS FROM THE RELEVANT AUTHORITIES. THE DRAWING IS TO BE USED FOR THE SPECIFIC PROJECT AND SITE ONLY. ANY REUSE OR MODIFICATION OF THIS DRAWING WITHOUT THE WRITTEN CONSENT OF THE DEVELOPER IS STRICTLY PROHIBITED.

PROJECT:
LOT 27 TRAVELLERS WAY
7 TRAVELLERS WAY TAHMOOR

DRAWING TITLE:
COVER SHEET

NORTH:

LOT NO:
27

CHECKED BY:
AS

DRAWN BY:
RH

SCALE
As indicated

DRAWING NO.
CC.01

REVISION
7

CC ISSUE

CLIENT NAME
Pratichya Tripathi & Samudra Nepal

TERMITE SHEET

- TERMITE SHEET EXTENDS THROUGH THE ENTIRE MASONRY LEAF AND IS VISIBLE AT THE FINISHED FACE OF THE WALL.


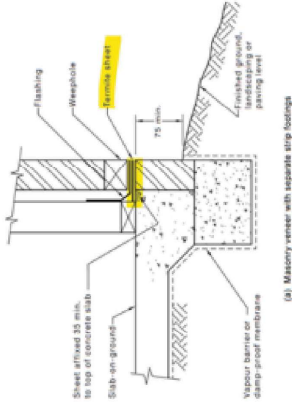


FIGURE 5.5 (in part). TYPICAL SHEET INSTALLATION TO EXTERNAL WALL WITH CONCRETE FLOOR SLAB

DPC FOR BRICKS

- DAMP-PROOF COURSE (DPC) TO EXTENDS THROUGH THE ENTIRE MASONRY LEAF AND NEED TO BE VISIBLE AT THE FINISHED FACE OF THE WALL FROM OUTSIDE

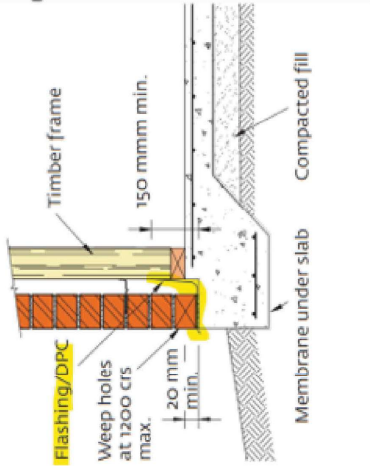

DEMOLITION

- AS 2601-2001 – DEMOLITION WORK

PLANTER BOX

REFER BELOW DETAILS FOR PLANTER BOX.


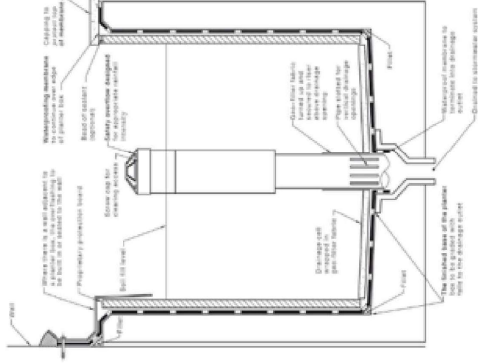


FIGURE 2.17 TYPICAL PLANTER BOX CONSTRUCTION

OVERFLOW TO BALCONY:

- SURFACE DRAIN & OVERFLOW TO BALCONY

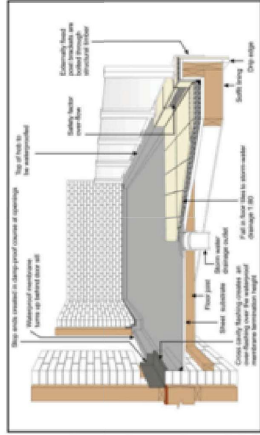

SWIMMING POOL

- PART 12.1.1 (H7D2) OF THE NCC VOLUME 2, AMENDMENT 1 – BUILDING CODE OF AUSTRALIA 2022 & HOUSING PROVISIONS STANDARD 2022
- AS 1926 PART 1-2012 – SWIMMING POOLSAFETY- SAFETY BARRIERS FOR SWIMMING POOLS
- AS 1926 PART 2-2007 - SWIMMING POOL SAFETY- LOCATION OF SAFETY BARRIERS FOR SWIMMING POOLS (INCORPORATING AMENDMENTS 1 AND 2)
- AS 1926 PART 3-2010 – SWIMMING POOL SAFETY- WATER RECIRCULATION SYSTEMS (INCORPORATING AMENDMENT 1)

REV	DATE	DESCRIPTION	BY
7	15-09-2026	CC ISSUE	
6	6-05-2026	DA ISSUE	



THIS DRAWING IS THE SOLE PROPERTY OF THE DEVELOPER. THE DEVELOPER'S ACCEPTANCE OF ANY PARTS WITHOUT THE WRITTEN CONSENT OF THE DEVELOPER IS A VIOLATION OF APPLICABLE LAW. 

PROJECT:

LOT 27 TRAVELLERS WAY

7 TRAVELLERS WAY TAHMOOR

DRAWING TITLE:

GENERAL NOTES

NORTH:

LOT NO.	DATE	SCALE	CC ISSUE
27	23-09-2026	1 : 2	
DRAWN BY:	CHECKED BY:	ISSUED BY:	
AS	RH	CC.02B	
DRAFTED BY:	CLIENT NAME		
SL	Pratichya Tripathi & Samudra Nepal		

OnBuild Certifiers Pty Ltd

Reference: 260060

Date: 01/10/2026

Andrew Soliman

Director/ Principal Certifier

BDC2940

Consultant who prepared this document remains responsible for accuracy

TRAVELLERS WAY



1 : 200

CODE COMPLIANCE TABLE					COMPLIANCE	COMMENT
Woolondilly Development Control Plan 2016-Volume 4 – Residential Development						
DESCRIPTION		CODE CONTROL	REQUIREMENT	PROPOSED		
ELEMENT		R2 – Low Density Residential				
LAND ZONE		LOT 27				
LOT NO		LOT AREA	450.0 m2			
LOT WIDTH		Standard Lot Min. 6m at Building Line facing primary road	6.0m	21.2 m	YES	
HEIGHT		MAX. Height	9m	5.55m (MAX.)	YES	
FRONT SETBACK		FRONT SET BACK (Min. Setback from Primary Road)	4.5 m	4.5m	YES	
REAR SET		GROUND FLOOR	3m	3.1m	YES	
SIDE SET		GROUND FLOOR	8m	NA	YES	
BACK (MIN.)		GROUND FLOOR	0.9/0.9m	0.9/5.2m	YES	
		FIRST FLOOR	0.9/0.9m	NA		
COVERAGE AREA		The total portion of the site covered by buildings shall not exceed 50% of the site area.	270SQM(60%)	121SQM(26.9%)	YES	
PRIVATE OPEN SPACE			18m2	24 m2	YES	
LANDSCAPE AREA				233.7 m2		

[illegible]

PROJECT:
LOT 27 7 TRAVELLERS
WAY
7 TRAVELLERS WAY TAHMOOR

DRAWING TITLE:
**LOCATION PLAN
AND SITE PLAN**

NORTH:		LOT NO:	27
		DRAWN BY:	AS
		DRAFTED BY:	SL

CC ISSUE		REV. 7
DATE: 23-09-2026	SCALE: As indicated	DRAWING NO. CC.03
CHECKED BY: HR	ISSUED BY:	
CLIENT NAME: Pratichhya Tripathi & Samudra Nepal		

Consultant who prepared this document
remains responsible for accuracy



1 : 200

DESCRIPTION



DRAWING TITLE:
**SITE CUT & FILL
PLAN**



ALE:

DRAWING No.:	REV.:	7
--------------	-------	---


Pratichh

OnBuild Certifiers Pty Ltd

SEDIMENT AND EROSION NOTES:
THIS PLAN TO BE BEACHIN 2600060
CONTROL MEASURES SHALL BE TAKEN TO PREVENT ALL SOIL EROSION AND SEDIMENT
THE CONSTRUCTION OF THE SITE SHALL BE IN ACCORDANCE WITH THE SAITSACTION OF
COUNCIL MEASURES AS NECESSARY AND TO THE SATISFACTION OF
COUNCIL. THE CONSTRUCTION OF THE SITE SHALL BE IN ACCORDANCE WITH THE
DISBURSANCE TO THE SITE SHALL BE PERMITTED OTHER THAN IN THE
IMMEDIATE AREA OF THE WORK. THE CONSTRUCTION OF THE SITE SHALL BE
FROM THE SITE WITHIN 100 MILES OF THE SITE. THE CONSTRUCTION OF THE SITE
EROSION CONTROL MEASURES SHALL BE INSTALLED AND MAINTAINED IN
CONFORMANCE WITH THE SAITSACTION OF COUNCIL MEASURES AS NECESSARY
AND TO THE SATISFACTION OF COUNCIL. THE CONSTRUCTION OF THE SITE
TOPSOIL SHALL BE STRIPPED AND STOCKPILED OUTSIDE OF HAZARDOUS AREAS
(SUCH AS DRAINAGE LINES). THIS TOPSOIL IS TO BE REPLACED LATER ON
AREAS TO BE REVEGETATED AND STABILISED ONLY. (IE ALL
FOOTPATHS BATTERS SITE REGARDING AREAS BASINS AND CATCH
DRAINS). TOPSOIL SHALL NOT BE RESPIRED ON ANY OTHER AREAS UNLESS
SPECIALLY INSTRUCTED BY THE SUPERINTENDENT. IF THEY ARE TO REMAIN FOR
USE ON THE SITE, THEY SHALL BE COVERED WITH A MOUND OF HYDROSEEDING AND IF
NECESSARY BY LOCATING BANKS OR DRAINS DOWNSTREAM OF A
CATCHMENT TO RETARD SILT LADEN RUNOFF.
THE CONTRACTOR SHALL REGULARLY MAINTAIN ALL SEDIMENT AND
EROSION CONTROL DEVICES AND REMOVE ACCUMULATED SILT FROM SUCH
DEVICES SUCH THAT MORE THAN 80% OF THEIR CAPACITY IS NOT LOST. ALL THE
SILTS TO BE PLACED OUTSIDE THE LIMIT OF WORKS. THE PERIOD FOR
THE CONSTRUCTION OF THE SITE SHALL BE IN ACCORDANCE WITH THE
AREAS ARE REVEGETATED AND FURTHER AS MAY BE DIRECTED BY THE
SUPERINTENDENT OR COUNCIL.
LAY TURF STRIP (MIN 300 mm WIDE) ON 100 mm TOPSOIL WITH 1.0 m LONG
RETURNS EVERY 6.0m BEHIND ALL KERB AT THE TOP OF ALL BATTERS AND
AROUND STRUCTURES IMMEDIATELY AFTER BACKFILLING OR FORMATION.
THE CONTRACTOR SHALL GRASS SEED ALL DISTURBED AREAS WITH AN
APPROVED MIX AS SOON AS PRACTICABLE AFTER COMPLETION OF
CONSTRUCTION OF THE SITE. THE CONTRACTOR SHALL MAINTAIN ALL
VEHICULAR TRAFFIC SHALL BE CONTROLLED DURING CONSTRUCTION
CONFINING ACCESS WHERE POSSIBLE TO NOMINATED STABILISED ACCESS
POINTS.
WHEN ANY DEVICES ARE TO BE HANDED OVER TO COUNCIL THEY SHALL BE
IN CLEAN AND STABLE CONDITION.
THE CONTRACTOR SHALL IMPLEMENT DUST CONTROL BY REGULAR
WETTING DOWN (BUT NOT SATURATING) UNDISTURBED AREA
AROUND THE PERIMETER OF THE SITE AND ALL SURFACE INLET PITS UNTIL
CATCHMENT IS REVEGETATED OR PAVED.
REVEGETATE ALL TRENCHES IMMEDIATELY UPON COMPLETION OF
BACKFILLING.
ALL DRAINAGE PIPE INLETS TO BE CAPPED UNTIL:
A) DOWNPIPES CONNECTED
B) PITS CONSTRUCTED & PROTECTED WITH SILT BARRIER


CONSTRUCTION WORKING AREAS TO BE MAINTAINED AND PROTECTED
TOPSOIL SHALL BE STRIPPED AND STOCKPILED OUTSIDE OF HAZARDOUS AREAS
(SUCH AS DRAINAGE LINES). THIS TOPSOIL IS TO BE REPLACED LATER ON
AREAS TO BE REVEGETATED AND STABILISED ONLY. (IE ALL
FOOTPATHS BATTERS SITE REGARDING AREAS BASINS AND CATCH
DRAINS). TOPSOIL SHALL NOT BE RESPIRED ON ANY OTHER AREAS UNLESS
SPECIALLY INSTRUCTED BY THE SUPERINTENDENT. IF THEY ARE TO REMAIN FOR
USE ON THE SITE, THEY SHALL BE COVERED WITH A MOUND OF HYDROSEEDING AND IF
NECESSARY BY LOCATING BANKS OR DRAINS DOWNSTREAM OF A
CATCHMENT TO RETARD SILT LADEN RUNOFF.
THE CONTRACTOR SHALL REGULARLY MAINTAIN ALL SEDIMENT AND
EROSION CONTROL DEVICES AND REMOVE ACCUMULATED SILT FROM SUCH
DEVICES SUCH THAT MORE THAN 80% OF THEIR CAPACITY IS NOT LOST. ALL THE
SILTS TO BE PLACED OUTSIDE THE LIMIT OF WORKS. THE PERIOD FOR
THE CONSTRUCTION OF THE SITE SHALL BE IN ACCORDANCE WITH THE
AREAS ARE REVEGETATED AND FURTHER AS MAY BE DIRECTED BY THE
SUPERINTENDENT OR COUNCIL.
LAY TURF STRIP (MIN 300 mm WIDE) ON 100 mm TOPSOIL WITH 1.0 m LONG
RETURNS EVERY 6.0m BEHIND ALL KERB AT THE TOP OF ALL BATTERS AND
AROUND STRUCTURES IMMEDIATELY AFTER BACKFILLING OR FORMATION.
THE CONTRACTOR SHALL GRASS SEED ALL DISTURBED AREAS WITH AN
APPROVED MIX AS SOON AS PRACTICABLE AFTER COMPLETION OF
CONSTRUCTION OF THE SITE. THE CONTRACTOR SHALL MAINTAIN ALL
VEHICULAR TRAFFIC SHALL BE CONTROLLED DURING CONSTRUCTION
CONFINING ACCESS WHERE POSSIBLE TO NOMINATED STABILISED ACCESS
POINTS.
WHEN ANY DEVICES ARE TO BE HANDED OVER TO COUNCIL THEY SHALL BE
IN CLEAN AND STABLE CONDITION.
THE CONTRACTOR SHALL IMPLEMENT DUST CONTROL BY REGULAR
WETTING DOWN (BUT NOT SATURATING) UNDISTURBED AREA
AROUND THE PERIMETER OF THE SITE AND ALL SURFACE INLET PITS UNTIL
CATCHMENT IS REVEGETATED OR PAVED.
REVEGETATE ALL TRENCHES IMMEDIATELY UPON COMPLETION OF
BACKFILLING.
ALL DRAINAGE PIPE INLETS TO BE CAPPED UNTIL:
A) DOWNPIPES CONNECTED
B) PITS CONSTRUCTED & PROTECTED WITH SILT BARRIER

TRAVELLERS WAY

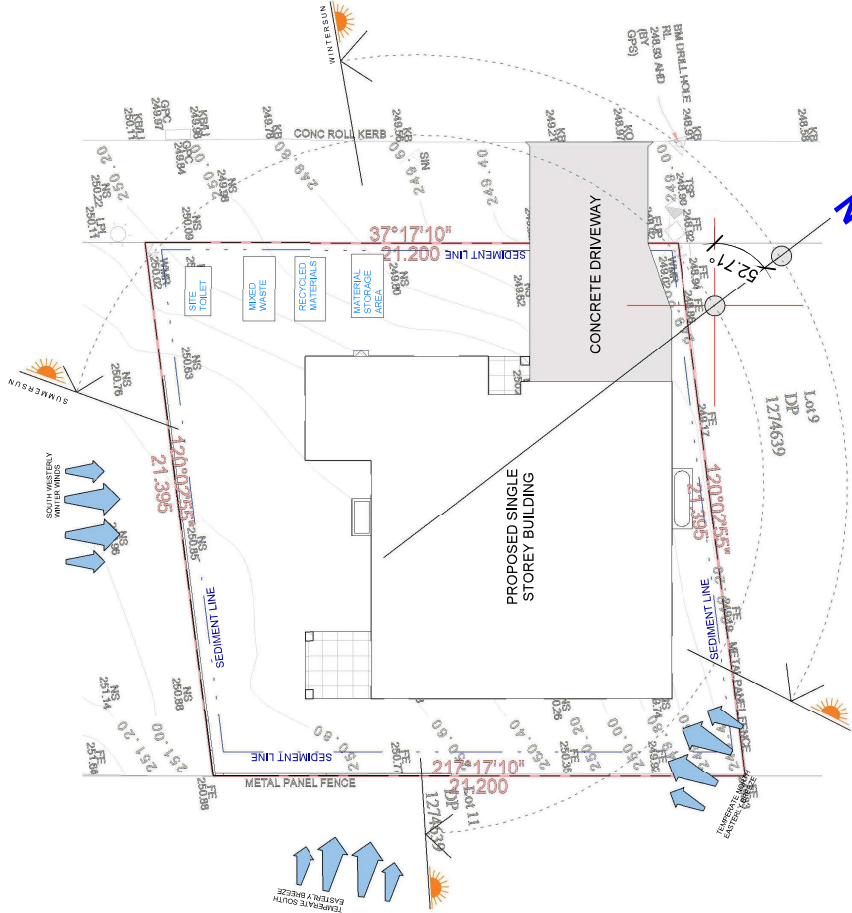

CC - SITE ANALYSIS AND SEDIMENT CONTROL PLAN

1:200

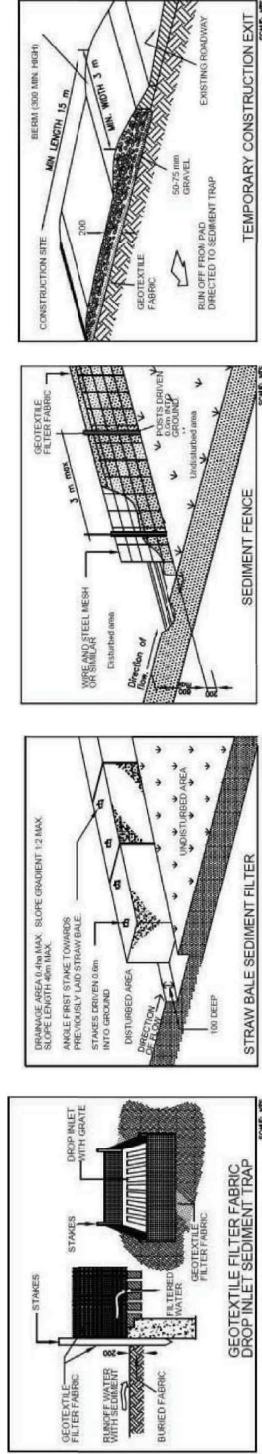

- SITE WORKS NOTES
1. CHECK OF LEVELS PROVIDED BY SURVEYOR
 2. THE BUILDER SHALL VERIFY ALL DIMENSIONS AND EXISTING LEVELS ON THE SITE. ANY DISCREPANCIES SHALL BE REPORTED TO THE SURVEYOR/ENGINEER
 3. TOPSOIL SHALL BE STRIPPED FROM THE CONSTRUCTION AREA AND STOCKPILED ON SITE. TO BE LATER SPREAD OR DISPOSED OFF SITE AS DIRECTED BY SUPERINTENDENT OR COUNCIL
 4. ALL SERVICE TRENCHES UNDER VEHICULAR PAVEMENTS SHALL BE REVEGETATED IMMEDIATELY UPON COMPLETION OF CONSTRUCTION. THE UNDERSEAL OF THE PAVEMENT, AND COMPACTED TO BR5 STANDARD MAXIMUM DENSITY, IN ACCORDANCE WITH AS 12881.1.
 5. ALL SERVICE TRENCHES UNDER VEHICULAR PAVEMENTS SHALL BE REVEGETATED IMMEDIATELY UPON COMPLETION OF CONSTRUCTION. THE UNDERSEAL OF THE PAVEMENT, AND COMPACTED TO BR5 STANDARD MAXIMUM DENSITY, IN ACCORDANCE WITH AS 12881.1.
- SD 5.7 STABILISED SITE ACCESS
- 1) STRIP TOPSOIL AND LEVEL SITE.
 - 2) COVER AREA WITH GEOTEXTILE.
 - 3) COVER AREA WITH GEOTEXTILE.
 - 4) CONSTRUCT 200 mm THICK PAD OVER GEOTEXTILE USING 50-75 mm GRAVEL.
 - 5) CONSTRUCT 200 mm THICK PAD OVER GEOTEXTILE USING 50-75 mm GRAVEL.
 - 6) CONSTRUCT 200 mm THICK PAD OVER GEOTEXTILE USING 50-75 mm GRAVEL.
 - 7) CONSTRUCT 200 mm THICK PAD OVER GEOTEXTILE USING 50-75 mm GRAVEL.
 - 8) CONSTRUCT 200 mm THICK PAD OVER GEOTEXTILE USING 50-75 mm GRAVEL.
 - 9) CONSTRUCT 200 mm THICK PAD OVER GEOTEXTILE USING 50-75 mm GRAVEL.
 - 10) CONSTRUCT 200 mm THICK PAD OVER GEOTEXTILE USING 50-75 mm GRAVEL.
- SD 5.9 GEOTEXTILE INLET FILTER
- 1) FABRICATE A SEDIMENT BARRIER MADE FROM GEOTEXTILE.
 - 2) SUPPORT GEOTEXTILE WITH MESH TIED TO POSTS AT 1m DIA.
 - 3) DO NOT COVER INLET WITH GEOTEXTILE.

CC ISSUE		DATE	SCALE	LOT NO	NORTH	DRAWING TITLE	PROJECT
7		23-09-2026	As indicated	27	AS	SITE ANALYSIS AND SEDIMENT CONTROL	LOT 27 TRAVELLERS WAY
CC.05		CHECKED BY	AS	DRAWN BY	AS	7 TRAVELLERS WAY TAHMOOR	7 TRAVELLERS WAY TAHMOOR
CLIENT NAME		PRATCHHYA TRIPATHI & SAMUDRA NEPAL					

REV	DATE	DESCRIPTION	BY
7	15-09-2026	CC ISSUE	
6	6-09-2026	DA ISSUE	

DATE	DESCRIPTION	ISSUED BY
23-09-2026	CC.05	CC.05


DATE	DESCRIPTION	ISSUED BY
23-09-2026	CC.05	CC.05

DATE	DESCRIPTION	ISSUED BY
23-09-2026	CC.05	CC.05

[illegible]

DETAILS SHOWN ON THE PLANS ARE INTENDED TO BE ACCURATE. HOWEVER, BUILDER/SUPPLIER RESERVE THE RIGHT TO ADJUST THE MEASUREMENTS/ITEMS AS REQUIRED DUE TO SITE CONDITIONS.

THE MEASUREMENTS PROVIDED IS STRUCTURAL SIZES ONLY, NOT A FINISHED FLOOR SIZE.

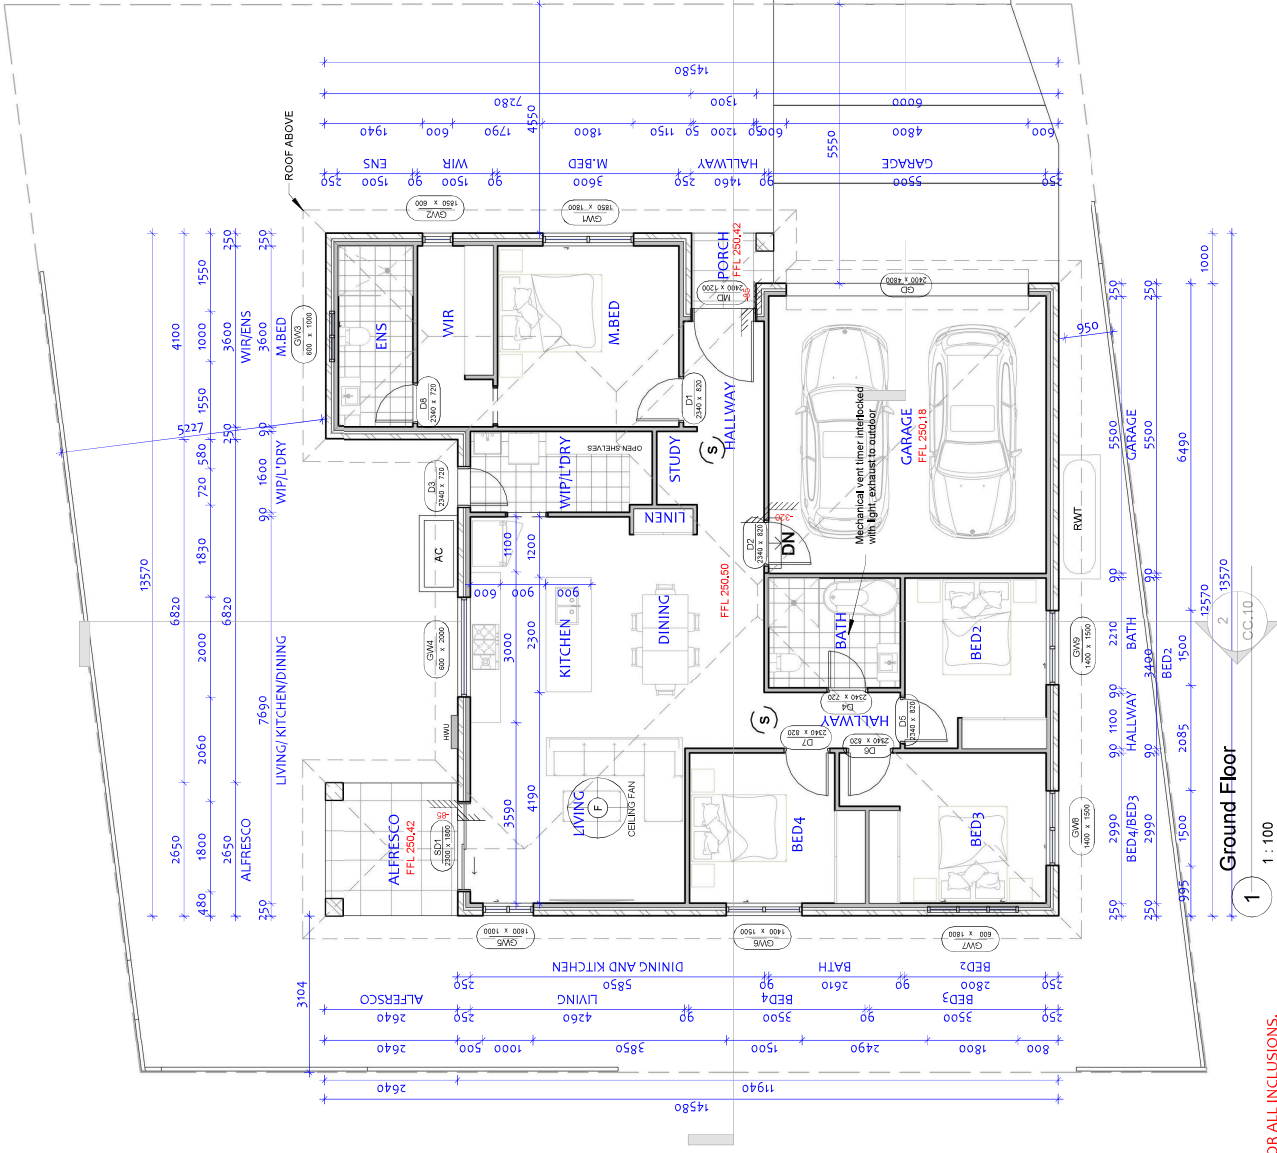

NOTE: PLEASE REFER TO TENDER FOR ALL INCLUSIONS.

REV	DATE	DESCRIPTION	BY
7	15-09-2026	CC ISSUE	
6	6-05-2026	DA ISSUE	
5	04-06-2026	Window added to Living Room, Highlight window to Bed 3 -Eka	
4	10-05-2026	Affresco and Study Nook added, Linen Shifted - Client Meeting.	
3	25-05-2026	New Concept Plan	



THIS DRAWING IS THE EXCLUSIVE PROPERTY OF THE DEVELOPER & THE REPRODUCTION OF ANY PART WITHOUT THE PRIOR WRITTEN CONSENT OF THE DEVELOPER IS A VIOLATION OF APPLICABLE LAWS. THE DEVELOPER ASSUMES NO LIABILITY FOR THE USE OF THIS DIGITAL DATA OR CONSEQUENTIAL LIABILITY IN CONNECTION WITH THE USE OF THIS DIGITAL DATA RELEASED FROM THE DEVELOPERS OFFICE. THIS DRAWING IS TO BE UNDERSTOOD IN CONNECTION WITH THE STRUCTURAL, MECHANICAL, ELECTRICAL & / OR ANY OTHER CONSULTANT DOCUMENTATION AS MAY BE APPLICABLE TO THE PROJECT PRIOR TO THE START OF ANY WORKS AND FOR ITS DURATION.

PROJECT:
LOT 27 7 TRAVELLERS
WAY
7 TRAVELLERS WAY TAHMOOR

DRAWING TITLE:
GROUND
PLAN

NORTH: 

LOT NO:	27	DATE:	23-09-2026
DRAWN BY:	AS	CHECKED BY:	RH
DRAFTED BY:	SL	CLIENT NAME:	Pratichya T

SCALE:	1 : 100	DRAWING No.	CC-06	REV.	7
			ISSUED BY:		

Consultant who prepared this document remains responsible for the accuracy of the information provided. The Consultant shall be responsible for the accuracy of the information provided. The Consultant shall be responsible for the accuracy of the information provided.

DETAILS SHOWN ON THE PLANS ARE INTENDED TO PREPARED THIS DOCUMENT


spc HOWEVER, BUILDER SUPERVISOR RESE

THE MEASUREMENT ITEMS AS REQUIRE CONDITIONS.

THE MEASUREMENTS PROVIDED IS STD

THE MEASUREMENT IS PROVIDED IN SINGLES
A FINISHED FLOOR SIZE.

1000

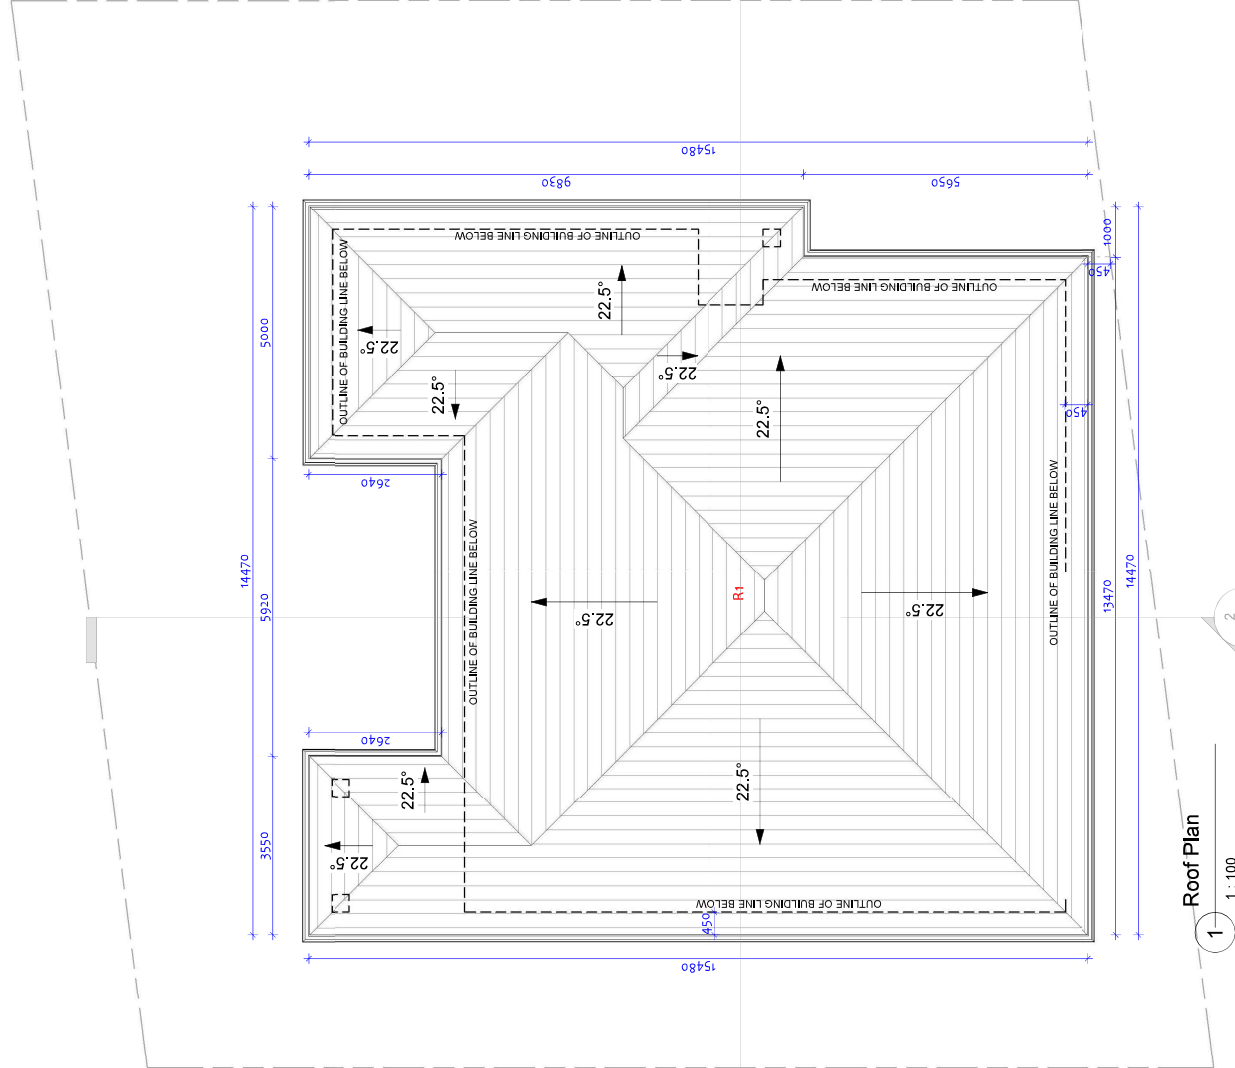

Roof Schedule			
Mark	Base Level	Area	Comments

R1	Ground Ceiling	219 m ²	TILE ROOF
----	----------------	--------------------	-----------

PLAN NORTH: 	LOT NO:	DATE:	SCALE:	DRAWING NO:	CC ISSUE
	27	23-09-2026	1 : 100	7	
	DRAWN BY:	CHECKED BY:			ISSUED BY:
	AS	RH		CC-07	
CLIENT NAME:					
SL					Pratichya Tripathi & Samudra Nepal

REV	DATE	DESCRIPTION	BY
7	15-09-2026	CC ISSUE	
6	6-08-2026	DA ISSUE	
5	04-06-2026	Window added to Living Room, Highlight window to Bed 3 -Ekta	