


Consultant who prepared this document
remains responsible for accuracy

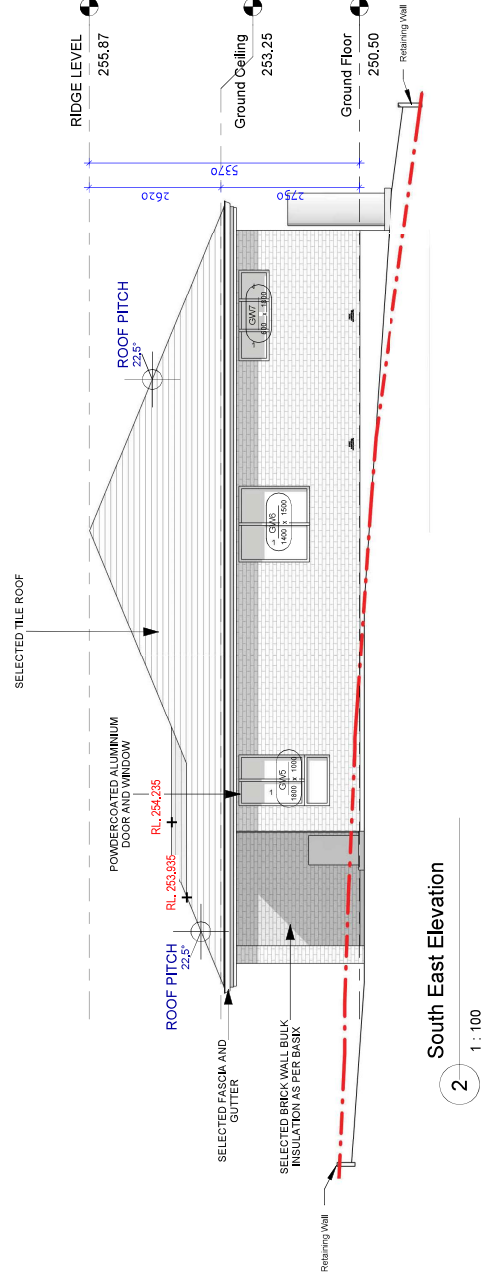

REV	DATE	DESCRIPTION	BY
7	15-09-2026	CC ISSUE	
6	6-08-2026	DA ISSUE	
5	04-06-2026	Window added to Living Room, Highlight window to Bed 3 -Ekt	

[illegible]

THIS DRAWING IS THE EXCLUSIVE PROPERTY OF THE DEVELOPER & THE REPRODUCTION OF ANY PART WITHOUT THE PRIOR WRITTEN CONSENT OF THE DEVELOPER IS A VIOLATION OF APPLICABLE LAWS. IN EVENT SHALL THE DEVELOPER BE HELD Liable FOR SPECIAL COLLATERAL INCIDENTAL DAMAGES. THIS DRAWING IS THE PROPERTY OF THE DEVELOPER & IS NOT TO BE REPRODUCED, COPIED, RELEASED FROM THE DEVELOPERS OFFICE. THIS DRAWING IS TO BE READ & UNDERSTOOD IN CONJUNCTION WITH THE STRUCTURAL, MECHANICAL, ELECTRICAL & FOR ANY OTHER CONSULTANT DOCUMENTATION AS MAY BE APPLICABLE TO THE PROJECT PRIOR TO THE START OF ANY WORKS AND FOR THIS DRAWING.

DRAWING TITLE:

ELEVATION 01



NORTH:

LOT NO:	27	DRAWN BY:	AS	DRAFTED BY:	SL
---------	----	-----------	----	-------------	----

DATE 23-09-2026		SCALE 1 : 100	CC.08 1 : 100	REV. 7	CC ISSUE 7
CHECKED BY RH				ISSUED BY	

OnBuild Certifiers Pty Ltd
Reference: 260060
Date: 01/10/2026
Andrew Soliman
Director/ Principal Certifier
BDC2940
Consultant who prepared this document
remains responsible for accuracy

Window Schedule 1					
Mark	Height	Width	Sill Height	Head Height	Description
Ground Floor					
GW1	1850	1800	550	2400	SLIDING
GW2	1850	600	550	2400	FIXED with AWNING
GW3	600	1000	1800	2400	SLIDING
GW4	600	2000	1050	1650	FIXED
GW5	1800	1000	600	2400	SLIDING
GW6	1400	1500	1000	2400	SLIDING
GW7	600	1800	1800	2400	SLIDING
GW8	1400	1500	1000	2400	SLIDING
GW9	1400	1500	1000	2400	SLIDING
Ground Floor: 9					

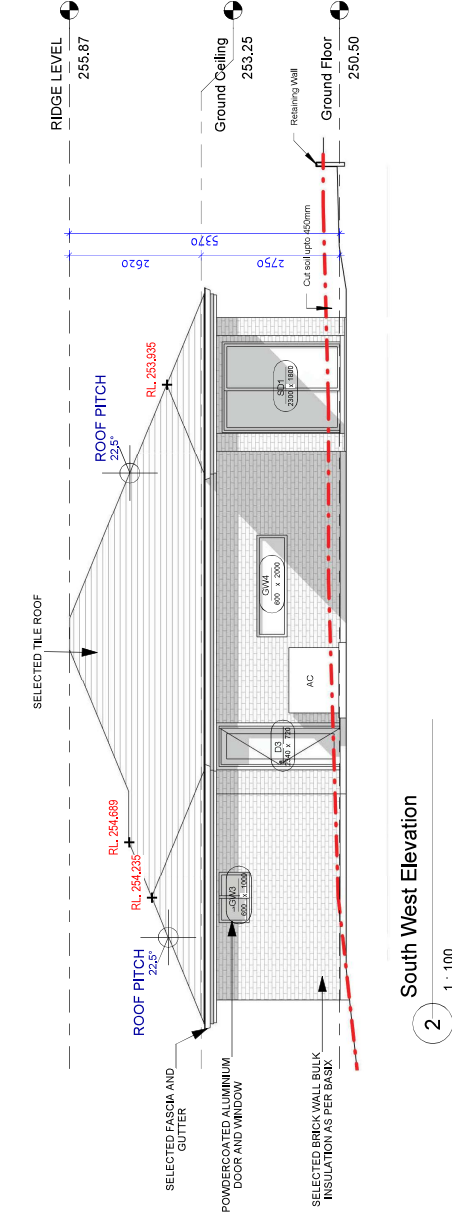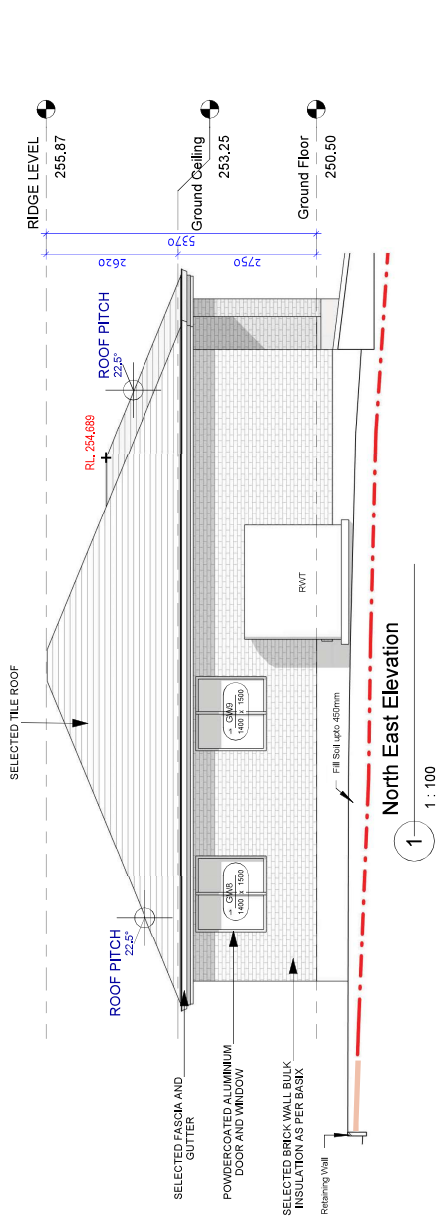

Door Schedule 1					
Mark	Height	Width	Count	Description	
Ground Floor					
D1	2340	820	1	FLUSH DOOR	
D2	2340	820	1	FLUSH DOOR	
D3	2340	720	1	FLUSH DOOR	
D4	2340	720	1	FLUSH DOOR	
D5	2340	820	1	FLUSH DOOR	
D6	2340	820	1	FLUSH DOOR	
D7	2340	820	1	FLUSH DOOR	
D8	2340	720	1	FLUSH DOOR	
GD	2400	4800	1	GARAGE DOOR	
MD	2400	1200	1	SOLID CORE DOOR	
SD1	2300	1800	1	SLIDING DOOR	
Ground Floor: 11					

REV	DATE	DESCRIPTION	BY
7	15-09-2026	CC ISSUE	
6	6-08-2026	DA ISSUE	
5	04-06-2026	Window added to Living Room. Highlight window to Bed 3 -Ektu	

RUBY HOMES

THIS DRAWING IS THE SOLE PROPERTY OF THE DEVELOPER. THE DEVELOPER'S USE OF ANY PART WITHOUT THE PRIOR WRITTEN CONSENT OF THE DEVELOPER IS A VIOLATION OF APPLICABLE LAW. CONsequential LIABILITY IS LIMITED TO THE USE OF THIS DATA FOR CONSTRUCTION. THE DRAWING IS NOT TO BE USED FOR ANY OTHER PURPOSES. 

PROJECT:
LOT 27 7 TRAVELLERS WAY
7 TRAVELLERS WAY TAHMOOR

DRAWING TITLE:
ELEVATION 02


NORTH:

LOT NO: 27
DATE: 23-09-2026
DRAWN BY: AS
CHECKED BY: RH
SCALE: 1 : 100

CC ISSUE
DRAWING NO: 7
ISSUED BY: CC.09
CLIENT NAME: Pratchhya Tripathi & Samudra Nepal


OnBuild Certifiers Pty Ltd
Reference: 260060
Date: 01/10/2026
Andrew Soliman
Director/ Principal Certifier
BDC2940

Consultant who prepared this document
remains responsible for accuracy

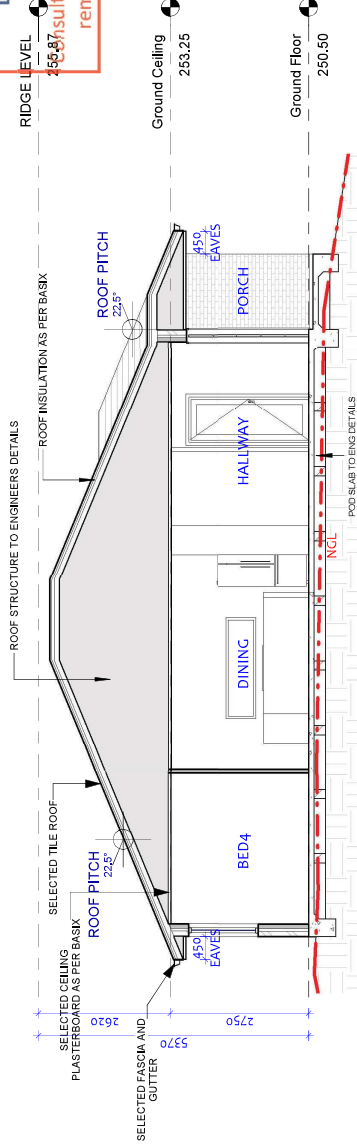

Section 1

1 1 : 100

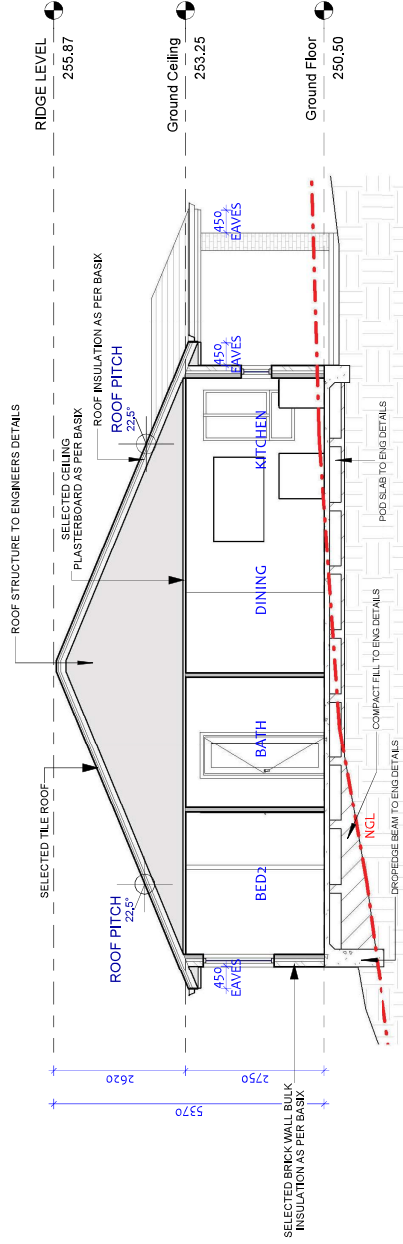

Section 2

2 1 : 100

REV	DATE	DESCRIPTION	BY
7	15-09-2026	CC ISSUE	
6	06-09-2026	DA ISSUE	



THIS DRAWING IS THE SOLE PROPERTY OF THE DEVELOPER. THE DEVELOPER'S PERMISSION IS REQUIRED FOR ANY REUSE OR REPRODUCTION OF THIS DRAWING. THE DEVELOPER'S PERMISSION IS NOT A GUARANTEE OF THE ACCURACY OF THE INFORMATION CONTAINED HEREIN. 

PROJECT:
LOT 27 TRAVELLERS
WAY
7 TRAVELLERS WAY TAHMOOR

DRAWING TITLE:
SECTIONS

NORTH:


LOT NO:	27
DRAWN BY:	AS
DRAFTED BY:	SL

DATE:	23-09-2026
CHECKED BY:	RH
CLIENT NAME:	Pratchhya Tripathi & Samudra Nepal

SCALE
1 : 100

CC ISSUE
DRAWING NO. REL. 7

Consultant who prepared this document
remains responsible for accuracy

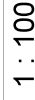

5
6
7
8
9
10
11
12


[illegible]

DATE:	23-09-2023
CHECKED BY:	RH
CLIENT NAME:	

DATE		SCALE	DRAWING NO.	REV.	7	CC ISSUE
23-09-2026						
CHECKED BY:			1 : 100	CC.11		ISSUED BY:
RH						
CLIENT NAME:						
Pratichhya Tripathi & Samudra Nepal						

Consultant who prepared this document
remains responsible for accuracy


Ground Floor: 2	151 m ²
Grand total: 2	151 m ²

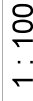[illegible]

DATE

A3

Consultant who prepared this document
remains responsible for accuracy

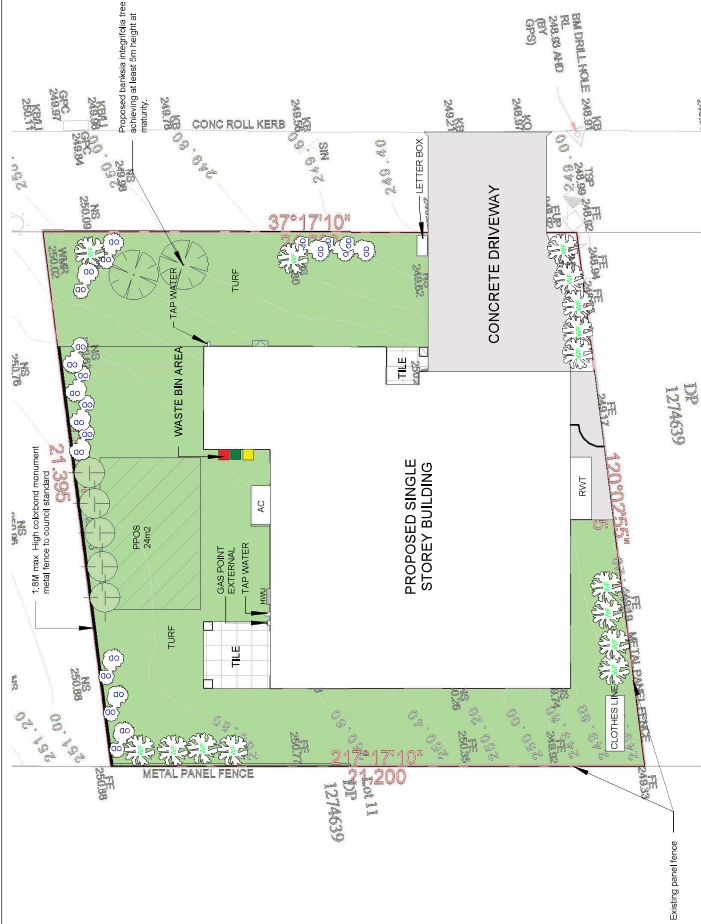

CC - LANDSCAPE PLAN

1 1 : 200

LANDSCAPE AREA	
FRONT AREA	68.8 m ²
BACKYARD AREA	164.9 m ²
TOTAL	233.7 m ²

PLANT SCHEDULE

Genus	Common Name	Qty	Pot size	Height	width
Trees					
Backhousia myrtifolia	Grey Myrtle	1	45L	6-10m	Dense feature tree with green glossy foliage. Greenish yellow flowers in small terminal clusters.
Shrubs					
Bursaria Spinosia Var Spinososa	Boxthorn	8	140mm	1.5m	Thorny, wiry branches. Leaf size and shape varies with age. Small, white fragrant flowers.
Dodonea Visco ssp. Cuneata	Wedge-Leaf Hop Bush	15	140mm	1m	Compact growth, sticky leaves taper to sharp point. Green fruit turns red and purple
Indigofera Australis	Native Indigo	5	140mm	1m	Slender, erect. Pink to lilac pea flowers, numerous along stems.
Hedging & screening Plants					
Acmencia anthilli 'Cherry Surprise'	Lilly Pilly Cherry Surprise	10	140mm	3m	It has attractive small dense green foliage that provides a continuous flush of cherry-red new growth nearly all year round. Small white starry flowers bloom in summer.

- GENERAL NOTES:**
- LANDSCAPE CONTRACTOR TO CHECK DA CONDITIONS AND STAMPED LANDSCAPE PLAN
 - BEFORE COMMENCING WORKS TO ENSURE NO EXISTING UTILITIES ARE AFFECTED
 - GARDEN BEDS IN OSD BASIN TO CONSIST OF NON FLOATABLE DECORATIVE GRAVEL
 - REFER TO HYDRAULICS ENGINEERS PLAN FOR OSD MULCH PLANTING BEDS TO BE A MINIMUM DEPTH OF 75mm AS SELECTED.
 - CONTRACTOR'S RESPONSIBILITY TO CHECK AND ADJUST BEDS/PATHWAYS TO BE PROVIDED TO ALL AREAS
 - FENCING/GATES TO DEFINE TURF AND GARDEN TURF/GARDEN TURF GRAVEL PATHS ETC.
 - WEEK MAT BENEATH GRAVEL PATHWAYS REQUIRED TO LIMIT MUD TRACKING.
 - ALL PLANTS TO BE HEALTHY AND VIGOROUS.
 - CONTRACTOR TO MAKE GOOD TURF ON NATURE STRIP POST CONSTRUCTION
 - CONTRACTOR TO MAKE GOOD TURF ON NATURE STRIP POST CONSTRUCTION.
 - DO NOT SCALE ARCHITECTURAL SETOUT FROM LANDSCAPE DRAWING.
 - PLANTING TREES SPREAD APPROXIMATE ONLY, REFER TO TREE SITE SURVEY PROVIDED BY OTHERS.
 - REPORT WHEN APPLICABLE.
 - BUFFALO TURF PREFERRED OVER KIKUYU.

LANDSCAPE BASK NOTE:
LANDSCAPE CONTRACTOR TO CHECK DA CONDITIONS AND STAMPED LANDSCAPE PLAN
BEFORE COMMENCING WORKS TO ENSURE NO EXISTING UTILITIES ARE AFFECTED
GARDEN BEDS IN OSD BASIN TO CONSIST OF NON FLOATABLE DECORATIVE GRAVEL
REFER TO HYDRAULICS ENGINEERS PLAN FOR OSD MULCH PLANTING BEDS TO BE A MINIMUM DEPTH OF 75mm AS SELECTED.

NOTE: BUILDER RESERVES THE RIGHT NOT TO UNDERTAKE NOR SUPPLY CERTIFICATE FOR NOTE: TO AID COMPLIANCE WITH BASIX LEGISLATION PLANTS (WHERE APPLICABLE) HAVE BEEN SELECTED FROM THE LOCAL CITY COUNCIL SHIRE PLANT LISTS.

NOTE: LOCATION OF SEWER MAINS, WATER PIPES UNDERGROUND ELECTRICITY AND OTHER SERVICES MUST BE OBTAINED PRIOR TO COMMENCEMENT OF ANY WORK ON SITE.

CONTRACTORS NOTE: CALCULATED AREAS DETERMINED BY CAD AND HAVE BEEN ROUNDED UP FOR USE AS A GUIDE ONLY ALLOW STANDARD PERCENTAGE FOR CUTTING AND WASTAGE. CONFIRM DIMENSIONS AND NUMBERS PRIOR TO QUOTING ORDERING.

REV	DATE	DESCRIPTION	BY
7	15-09-2026	CC ISSUE	
6	6-08-2026	DA ISSUE	

RUBY HOMES

THIS DRAWING IS THE SOLE PROPERTY OF RUBY HOMES. IT IS TO BE USED ONLY FOR THE PROJECT AND SITE SPECIFICALLY IDENTIFIED. ANY REUSE OR MODIFICATION OF THIS DRAWING WITHOUT THE WRITTEN CONSENT OF RUBY HOMES IS STRICTLY PROHIBITED. RUBY HOMES ACCEPTS NO LIABILITY FOR CONSEQUENTIAL DAMAGES ARISING FROM THE USE OF THIS DRAWING. CONSULT WITH THE STRUCTURAL, MECHANICAL, ELECTRICAL, OR ANY OTHER CONSULTANT PRIOR TO COMMENCEMENT OF ANY WORK. DOCUMENTATION AS MAY BE APPLICABLE AND ON THE DRAWING.

PROJECT:
LOT 27 7 TRAVELLERS WAY
7 TRAVELLERS WAY TAHMOOR

DRAWING TITLE:
LANDSCAPE PLAN


NORTH:

LOT NO: 27
DRAWN BY: AS
CHECKED BY: RH
DATE: 23-09-2026
SCALE: 1:200

CC ISSUE
DRAWING NO: REL 7
ISSUED BY: CC.15
CLIENT NAME: Pratchiya Tripathi & Samudra Nepal


OnBuild Certifiers Pty Ltd
Reference: 260060
Date: 01/10/2026
Andrew Solomon
Director/ Principal Certifier
BDC2940
Consultant who prepared this document remains responsible for accuracy

- LEGENDS**
- PROPOSED SCREENING PLANTING
 - PROPOSED SHRUB PLANTING
 - PROPOSED ACCENT PLANTING
 - PROPOSED TREE
 - PROPOSED TURF AREA TO BE SIR WALTER SOFT LEAF BUFFALO
 - PROPOSED CONCRETE PATH

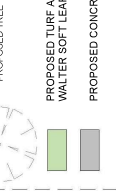

1. TURF & GARDEN EDGE DETAIL

NOTE:
DOWNSIDE OF BENCH SHALL BE GIVEN A FREE FROM DOWNSIDE PLANTING

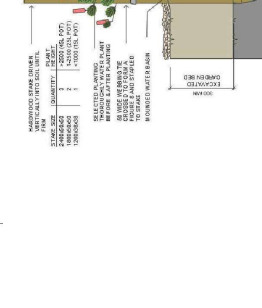

2. TREE & SHRUB PLANTING IN GARDEN BED

NOTE:
DOWNSIDE OF BENCH SHALL BE GIVEN A FREE FROM DOWNSIDE PLANTING

- Bursaria spinosa**
Type: Spinosia
Description: Shrub, very branches, leaf size and shape varies with age. Small, white fragrant flowers. Propagation: cut from seed or stake cutting a year after flowering, only to maintain shape.
- Dodonea viscosa ssp. cuneata**
Type: Shrub
Description: Compact growth, sticky leaves taper to sharp point. Green fruit turns red and purple. Propagation: cut from seed or stake cutting a year after flowering, only to maintain shape.
- Indigofera australis**
Type: Shrub
Description: Slender, erect. Pink to lilac pea flowers, numerous along stems. Propagation: cut from seed or stake cutting a year after flowering, only to maintain shape.
- Backhousia myrtifolia**
Type: Tree
Description: Dense feature tree with green glossy foliage. Greenish yellow flowers in small terminal clusters. Propagation: cut from seed or stake cutting a year after flowering, only to maintain shape.

ABCB HOUSING PROVISIONS : PART 10.2 WET AREA WATERPROOFING

10.2.1 Wet Areas

1. Building elements in wet areas within a building must be protected with a waterproofing system.
2. The waterproofing system in (1) must be either waterproof or water resistant in accordance with 10.2.2 to 10.2.6.

10.2.2 Shower Area (enclosed and unenclosed)

1. For a shower area with a hob, step-down or level threshold, the following applies:
- a. The floor of the shower area must be waterproof, including any hob or step-down (see Figure 10.2.2); and
- b. The walls of the shower area must be waterproof not less than 1800 mm above the floor substrate.
2. For a shower area with a level threshold, the following applies:
- a. Wall junctions and joints within the shower area must be waterproof not less than 40 mm either side of the junction (see Figure 10.2.2);
- b. Wall-floor junctions within the shower area must be waterproof (see Figure 10.2.2);
- c. Penetrations in the shower area must be waterproof (see Figure 10.2.2);
- d. A shower with a performed shower base must also comply with the requirements of (1), except for (a) which is not applicable.

Figure 10.2.2: Extent of treatment for shower areas - concrete compressed fibre-cement and fibre-cement sheet floors.

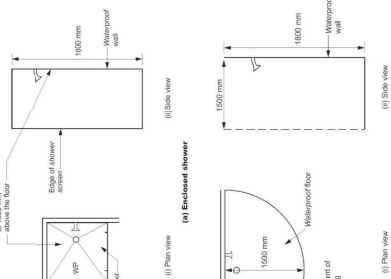


Figure Notes
Wall-floor junction heights are to be as per 10.2.2 to 10.2.6 (as applicable).

Notes

Where a shower is above a bath or spa, use requirements for shower.

10.2.3 Area outside shower area

1. For concrete, compressed fibre-cement and fibre-cement sheet flooring, the floor of the room must be water resistant.
2. For timber floors including particleboard, plywood and other timber based flooring materials, the floor of the room must be waterproof.
3. Wall-floor junctions must be:
- a. waterproof, and
- b. where a flashing is used, the horizontal leg must be not less than 40 mm.


10.2.4 Areas adjacent to baths and spas without showers

1. For areas adjacent to all baths and spas, the following applies:
- a. For concrete, compressed fibre-cement and fibre-cement sheet flooring, the floor of the room must be water resistant.
- b. For timber floors including particleboard, plywood and other timber based flooring materials, the floor of the room must be waterproof.
- c. For areas adjacent to baths and spas, the following applies:
- a. Walls must be water resistant (see Figure 10.2.4a and Figure 10.2.4b) to a height of not less than 1500 mm above the vessel, for the extent of the vessel, where the vessel is within 750 mm of a wall, and
- b. Wall-floor junctions and joints must be waterproof for the extent of the vessel.
2. For inserted baths and spas, the following applies:
- a. For floors and walls, the following applies:
- Any shaft area adjoining the bath or spa must be waterproof and include a waterstop under the vessel lip.
- There are no requirements for the floor under a bath or spa.
- b. For walls:
- Waterproof to not less than 1500 mm above the lip of a bath or spa.
- There are no requirements for the floor under a bath or spa.
- c. For wall junctions and joints, the following applies:
- For wall junctions and joints, the following applies:
- There are no requirements for junctions and joints in walls beneath the lip of a bath or spa.
- d. Tap and spout penetrations must be waterproof where they occur in horizontal surfaces.

10.2.5 Other areas

1. For walls adjoining other types of vessels and floors, the following applies:
- a. For walls adjoining other types of vessels and floors, the following applies:
- b. For walls adjoining other types of vessels and floors, the following applies:
- c. For walls adjoining other types of vessels and floors, the following applies:
2. For handholes and WCs, the following applies:
- a. For handholes and WCs, the following applies:
- b. For handholes and WCs, the following applies:
3. For WCs with handholes, the following applies:
- a. For WCs with handholes, the following applies:
- b. For WCs with handholes, the following applies:

Figure 10.2.5: Bath and vessel abutting wall - areas to be protected

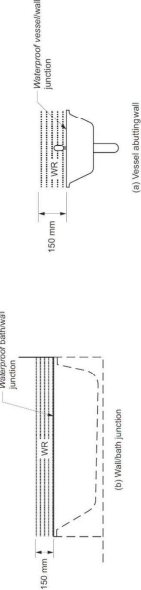

10.2.6 Waterproofing systems

1. For the purposes of this Part, a waterproofing system is deemed -
- a. waterproof, if it complies with (2), or
- b. water resistant, if it complies with (3).
2. For a waterproofing system required to be waterproof in accordance with 10.2.2 to 10.2.5, the materials nominated in 10.2.9 must be used.
3. For a waterproofing system required to be water resistant in accordance with 10.2.2 to 10.2.5, the materials nominated in 10.2.9 must be used in conjunction with the materials in 10.2.10.

10.2.12 Construction of wet area floors - falls

Where a floor waste is installed -

a. the minimum continuous fall of a floor plane to the waste must be 1:80, and

b. the maximum continuous fall of a floor plane to the waste must be 1:50.

REV	DATE	CC ISSUE	DESCRIPTION	BY
7	15-09-2026	CC ISSUE		



THE DRAWING IS THE SOLE PROPERTY OF THE ISSUERS. THE REPRODUCTION OF ANY PART WITHOUT THE PERMITTED WRITTEN CONSENT OF THE ISSUERS IS A VIOLATION OF APPLICABLE LAWS. CONsequential LIABILITY IN CONNECTION WITH THE USE OF THIS DATA DOCUMENT IS CONFINED TO THE ISSUERS. THE ISSUERS ACCEPT NO LIABILITY FOR ANY OTHER CONSEQUENCES OF THE USE OF THIS DATA DOCUMENT. THE ISSUERS ACCEPT NO LIABILITY FOR ANY OTHER CONSEQUENCES OF THE USE OF THIS DATA DOCUMENT.

PROJECT:

LOT 27 7 TRAVELLERS WAY

7 TRAVELLERS WAY TAHMOOR

DRAWING TITLE:

WATERPROOFING DETAILS

NORTH:

LOT NO:	DATE:	SCALE:	CC ISSUE
27	23-09-2026	1 : 50	CC.17
DRAWN BY:	CHECKED BY:	ISSUED BY:	
Author	RH		
DRAFTED BY:	CLIENT NAME:		
ID	Pratichhya Tripathi & Samudra Nepal		

OnBuild Certifiers Pty Ltd

Reference: 260060

Date: 01/10/2026

For walls adjoining other types of vessels and floors, the following applies:

a. For walls adjoining other types of vessels and floors, the following applies:

b. For walls adjoining other types of vessels and floors, the following applies:

c. For walls adjoining other types of vessels and floors, the following applies:

2. For handholes and WCs, the following applies:

a. For handholes and WCs, the following applies:

b. For handholes and WCs, the following applies:

3. For WCs with handholes, the following applies:

a. For WCs with handholes, the following applies:

b. For WCs with handholes, the following applies: