
FOR CONSTRUCTION

PROPOSED CONSTRUCTION OF A TWO STOREY DWELLING

LOT 42 IN DP 1276530, LOCATED AT
NO. 52, DRINKWATER AVENUE, ROUSE HIL

PARAGON
Paragon Building Certifiers Pty Ltd
RBC00045
Registered Certifier
APPROVED
Reference: 260258/01
Date: 10/06/2026

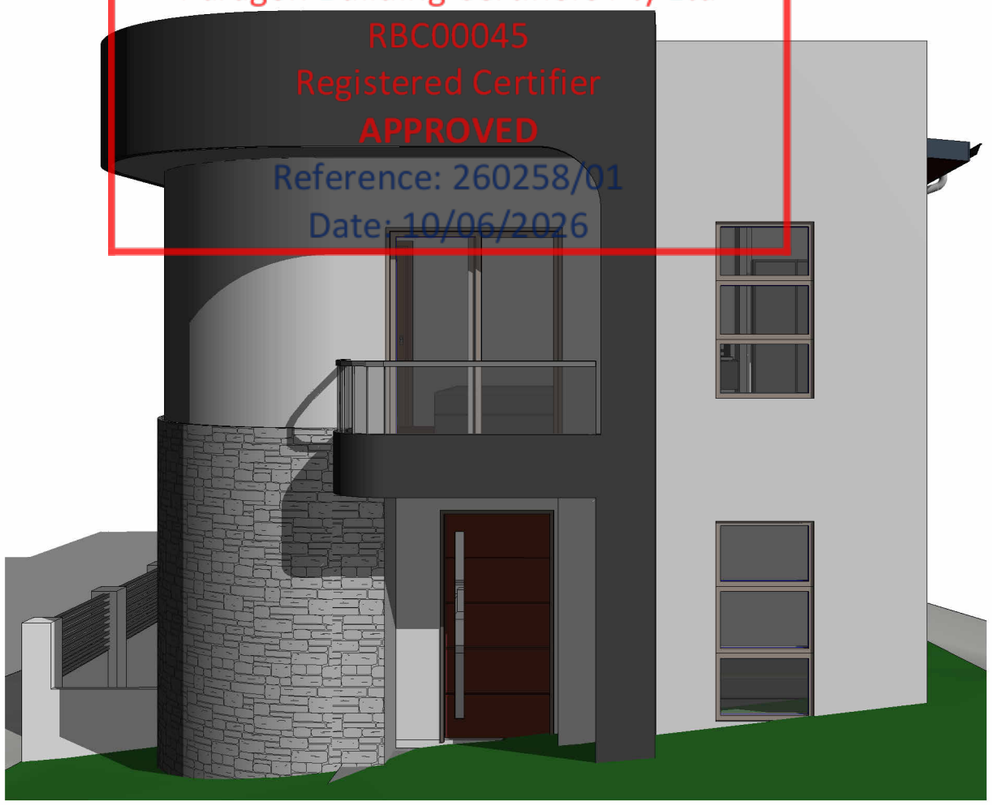

BASIX COMMITMENTS	Certificate number: 1741551S_04 Date of issue: Friday, 13 June 2025
WATER	
LANDSCAPE	81m2
TOILETS	4 STARS
KITCHEN TAPS	4 STARS
SHOWER HEADS	4 STAR (>4.5 but <=6 Umin)
BASIN TAPS	4 STARS
ALTERNATIVE WATER	2000L RAINWATER TANK
ROOF WATER TO TANK	159m2
ALT.WATER USES- TANK	LAUNDRY
ALT. WATER USES - RETIC	ALL TOILETS + ONE OUTDOOR TAP
SWIMMING POOL	N/A
ENERGY	
HOT WATER	GAS INSTANTANEOUS - 5 STAR
AIR-CON (HEATING)	3 PHASE DUCTED - EER 3.0-3.5
AIR-CON (COOLING)	3 PHASE DUCTED - EER 3.0-3.5
VENTILATION - BATHROOM	NONE/ NATURAL VENTILATION
VENTILATION - KITCHEN	DUCTED - MANUAL SWITCH
VENTILATION - LAUNDRY	NONE/ NATURAL VENTILATION
PV SYSTEM	N/A
COOKTOP	GAS
OVEN	ELECTRIC
CLOTHES DRYING	OUTDOOR CLOTHESLINE
LIGHTING	DEDICATED LED

GENERAL LEGEND

AC	AIR CONDITIONING UNIT
AL	POWDERCOATED ALUMINIUM DOOR/ WINDOW
BAL	BALUSTRADE TYPE
BG	BOX GUTTER
BR1, BR2, etc.	BRICK FACE TYPE
CAP	METAL CAPPING
CD1, CD2, etc.	WALL CLADDING
CONC.	CONCRETE FLOOR
CPT	CARPET
CRT	CONCRETE ROOF TILES
CR1, CR2, etc.	CEMENT RENDER TYPE/ COLOUR
DP/S	DOWN PIPE
DW	DISH WASHER
ED	ENTRY DOOR
F	FRIDGE
FAS	FASCIA
FET	FEATURE TILE
FT, FT1, FT2, etc.	FLOOR TILES
FW	FLOOR WASTE
GD	GARAGE DOOR
GUT	GUTTER
HWU	HOT WATER UNIT
HYB	HYBRID FLOOR
L	LINEN
MR	METAL ROOF
MW	MICROWAVE OVEN
NGL	NATURAL GROUND LEVEL
OBS	OBSCURED GLASS
P	PANTRY
R	ROBE
RL	REDUCED LEVEL
RWH	RAIN WATER HEAD
RWT	RAIN WATER TANK
S	STORAGE
TOW	TOP OF WALL
TL	TIMBER LAMINATE
WC	WATER CLOSET
WM	WASHING MACHINE
SD	SMOKE DETECTOR

Sheet List

Sheet No.	Sheet Name	Drawn By	Current Revision Date	Revision
CC.01	COVER SHEET	AS	28-04-2026	CC ISSUE
CC.02A	GENERAL NOTES A	AS	28-04-2026	CC ISSUE
CC.03	LOCATION PLAN AND SITE PLAN	AS	28-04-2026	CC ISSUE
CC.04	SITE ANALYSIS AND SEDIMENT CONTROL	AS	28-04-2026	CC ISSUE
CC.05	GROUND FLOOR PLAN	AS	28-04-2026	CC ISSUE
CC.06	FIRST FLOOR LEVEL	AS	28-04-2026	CC ISSUE
CC.07	ROOF PLAN	AS	28-04-2026	CC ISSUE
CC.08	ELEVATION 01	AS	28-04-2026	CC ISSUE
CC.09	ELEVATION 02	AS	28-04-2026	CC ISSUE

Sheet List

Sheet No.	Sheet Name	Drawn By	Current Revision Date	Revision
CC.10	SECTIONS	AS	28-04-2026	CC ISSUE
CC.11	FLOOR AREA PLAN	AS	28-04-2026	CC ISSUE
CC.12	RENTABLE AREA PLAN	AS	28-04-2026	CC ISSUE
CC.13	ROOM AREA PLAN	AS	28-04-2026	CC ISSUE
CC.14	COLOR SCHEDULE	AS	28-04-2026	CC ISSUE
CC.15	LANDSCAPE PLAN	AS	28-04-2026	CC ISSUE
CC.16	BASIX	AS	28-04-2026	CC ISSUE
CC.17	DRIVEWAY PLAN	AS	28-04-2026	CC ISSUE
CC.02B	GENERAL NOTES B	AS	28-04-2026	CC ISSUE
CC.18	WATERPROOFING DETAILS	AS	28-04-2026	CC ISSUE

REV	DATE	DESCRIPTION	BY
1	28-04-2026	Revision 1	

THIS DRAWING IS THE EXCLUSIVE PROPERTY OF THE DEVELOPER & THE REPRODUCTION OF ANY PART WITHOUT THE PRIOR WRITTEN CONSENT OF THE DEVELOPER IS A VIOLATION OF APPLICABLE LAWS. IN NO EVENT SHALL THE DEVELOPER BE HELD LIABLE FOR SPECIAL COLLATERAL, INCIDENTAL OR CONSEQUENTIAL LIABILITY IN CONNECTION WITH THE USE OF THIS DIGITAL DATA ONCE RELEASED FROM THE DEVELOPER'S OFFICE. THIS DRAWING IS TO BE READ & UNDERSTOOD IN CONJUNCTION WITH THE STRUCTURAL, MECHANICAL, ELECTRICAL & / OR ANY OTHER CONSULTANT'S DOCUMENTATION AS MAY BE APPLICABLE TO THE PROJECT PRIOR TO THE START OF ANY WORKS AND FOR ITS DURATION.

RUBY HOMES

PROJECT:
52 DRINKWATER AVENUE
LOT 42 52 DRINKWATER AVENUE ROUSE HILL

DRAWING TITLE:
COVER SHEET

NORTH:

CC ISSUE

LOT NO:	DATE:	SCALE:	DRAWING No:	REV:
42	22-05-2024	As indicated	CC.01	1
DRAWN BY: AS	CHECKED BY: RH			ISSUED BY:
DRAFTED BY: SL	CLIENT NAME: Owner			

A3

BUILDING SPECIFICATIONS

National Construction Code – Volume 2, Amendment 1 – Building Code of Australia 2022 & Housing Provisions Standard 2022

PARAGON
Paragon Building Certifiers Pty Ltd
RBC00045
Registered Certifier
APPROVED
Reference: 260258/01
Date: 10/06/2026

SITE PREPARATION

- PART 3.1 OF THE NCC VOLUME 2, AMENDMENT 1 - BUILDING CODE OF AUSTRALIA 2022 & HOUSING PROVISIONS STANDARD 2022.

EARTHWORKS

- TO BE CARRIED OUT IN ACCORDANCE WITH THE REQUIREMENTS OF THE ENVIRONMENTAL PLANNING & ASSESSMENT ACT 1979 AND DEVELOPMENT CONSENT CONDITIONS
- PART 3.2 OF THE NCC VOLUME 2, AMENDMENT 1 - BUILDING CODE OF AUSTRALIA 2022 & HOUSING PROVISIONS STANDARD 2022.
- AS 4678:2002 - EARTH-RETAININGSTRUCTURES

DRAINAGE

- PART 3.3 OF THE NCC VOLUME 2, AMENDMENT 1 - BUILDING CODE OF AUSTRALIA 2022 & HOUSING PROVISIONS STANDARD 2022.
- AS/NZS 3500.1:2021 - PLUMBING & DRAINAGE - WATER SERVICES
- AS/NZS 3500.2:2021 - PLUMBING & DRAINAGE - SANITARY PLUMBING & DRAINAGE
- AS/NZS 3500.3:2021 - PLUMBING & DRAINAGE STORMWATER DRAINAGE
- AS/NZS 3500.4:2021 - PLUMBING & DRAINAGE - HEATED WATER SERVICES

STRUCTURAL WORK

- Part 2.2 OF THE NCC VOLUME 2, AMENDMENT 1 - BUILDING CODE OF AUSTRALIA 2022 & HOUSING PROVISIONS STANDARD 2022.
- AS 4100-2020– STEEL STRUCTURES CODES
- AS/NZS 1170.0-2002 – GENERAL PRINCIPLES
- ASNZS 1170.1-2002 – PARTS 1 PERMANENT, IMPOSED AND OTHER ACTIONS
- AS/NZS 1170.2-2021 – PART 2 WIND ACTIONS
- AS 3700-2018– SAA MASONRY CODE
- AS 1684.3-2021- RESIDENTIAL TIMBER FRAMED CONSTRUCTION

FOOTINGS & SLABS

- PART 4 OF THE NCC VOLUME 2, AMENDMENT 1 - BUILDING CODE OF AUSTRALIA 2022 & HOUSING PROVISIONS STANDARD 2022.
- AS 2159:2009 - PILING - DESIGN & INSTALLATION
- AS 2870:2011 - RESIDENTIAL SLABS & FOOTINGS
- AS 3600:2018 - CONCRETE STRUCTURES

MASONRY

- PART 5 OF THE NCC VOLUME 2, AMENDMENT 1 - BUILDING CODE OF AUSTRALIA 2022 & HOUSING PROVISIONS STANDARD 2022.
- AS 3700:2018 - MASONRY STRUCTURES

FRAMING

- PART 6 OF THE NCC VOLUME 2, AMENDMENT 1 - BUILDING CODE OF AUSTRALIA 2022 & HOUSING PROVISIONS STANDARD 2022.
- AS 1684.2:2021 - RESIDENTIAL TIMBER-FRAMED CONSTRUCTION - NON- CYCLONIC AREAS
- AS 1720.1:2010 - TIMBER STRUCTURES - DESIGN METHODS
- AS 4100:2020 - STEEL STRUCTURES
- AS 3660.1-2014 – TERMITE MANAGEMENT SYSTEM

ROOF & WALL CLADDING

- PART 7 OF THE NCC VOLUME 2, AMENDMENT 1 - BUILDING CODE OF AUSTRALIA 2022 & HOUSING PROVISIONS STANDARD 2022.
- AS 1273:1991 - UNPLASTICIZED PVC (UPVC) DOWNPIPES & FITTINGS FORRAINWATER
- AS 1562.1:2018 - DESIGN & INSTALLATION OF SHEET ROOF & WALL CLADDING - METAL
- AS/NZS 1562.3:2006 - DESIGN & INSTALLATION OF SHEET ROOF & WALL CLADDING - PLASTIC
- AS 2049:2002 - ROOF TILES
- AS 2050:2018 - INSTALLATION OF ROOF TILES
- AS 4285:2019 – ROOFLIGHTS

GLAZING

- PART 8 OF THE NCC VOLUME 2, AMENDMENT 1 - BUILDING CODE OF AUSTRALIA 2022 & HOUSING PROVISIONS STANDARD 2022.
- AS 1288:2021 - GLASS IN BUILDINGS -SELECTION & INSTALLATION
- AS 2047:2014 - WINDOWS & EXTERNAL GLAZED DOORS IN BUILDINGS
- AS/NZS 2208:1996 - SAFETY GLAZING MATERIALS IN BUILDINGS

FIRE SAFETY

- PART 9 OF THE NCC VOLUME 2, AMENDMENT 1 - BUILDING CODE OF AUSTRALIA 2022 & HOUSING PROVISIONS STANDARD 2022.
- AS 3786:2014 - SMOKE ALARMS USING SCATTERED LIGHT, TRANSMITTED LIGHTOR IONIZATION

HEALTH & AMENITY

- PART 10 OF THE NCC VOLUME 2, AMENDMENT 1 - BUILDING CODE OF AUSTRALIA 2022 & HOUSING PROVISIONS STANDARD 2022.
- AS/NZS ISO 717.1:2004 - ACOUSTICS - RATING OF SOUND INSULATION IN BUILDINGS & OF BUILDING ELEMENTS -AIRBORNE SOUND INSULATION
- AS ISO 717.2:2004 - ACOUSTICS - RATING OF SOUND INSULATION IN BUILDINGS & OF BUILDING ELEMENTS - IMPACT SOUND INSULATION
- AS 1668.2:2012 - THE USE OF VENTILATION & AIR CONDITIONING IN BUILDINGS - MECHANICAL VENTILATIONIN BUILDINGS
- AS 1668.4:2012 - THE USE OF VENTILATION & AIR CONDITIONING IN BUILDINGS - NATURAL VENTILATION OFBUILDINGS
- AS/NZS 1680.0:2009 - INTERIOR LIGHTING - SAFE MOVEMENT
- AS 3740:2021 - WATERPROOFING OF DOMESTIC WET AREAS
- AS 3000-2018 – ELECTRICAL INSTALLATION
- BCA Part 10.8.1, AS4200.1 & AS4200.2 – PLIABLE BUILDING MEMBRANE INSTALLED.

WATERPROOFING

- PART 10.2 OF THE NCC VOLUME 2, AMENDMENT 1 - BUILDING CODE OF AUSTRALIA 2022 & HOUSING PROVISIONS STANDARD 2022
- AS 3740-2021– WATERPROOFING TO WET AREA
- AS 4654-2012 – EXTERNAL WET AREAS

SAFE MOVEMENT & ACCESS

- PART 11 OF THE NCC VOLUME 2, AMENDMENT 1 - BUILDING CODE OF AUSTRALIA 2022 & HOUSING PROVISIONS STANDARD 2022.
- AS 1428.1:2009 - DESIGN FOR ACCESS &MOBILITY – GENERAL REQUIREMENTS FOR ACCESS - NEW BUILDING WORK
- AS 1657:2018 - FIXED PLATFORMS, WALKWAYS, STAIRWAYS & LADDERS - DESIGN, CONSTRUCTION & INSTALLATION

HANDRAILS & BALUSTRADE

- PART 11.3.3 OF THE NCC VOLUME 2, AMENDMENT 1 - BUILDING CODE OF AUSTRALIA 2022 & HOUSING PROVISIONS STANDARD 2022.
- PART 11.3.4 OF THE NCC VOLUME 2, AMENDMENT 1 - BUILDING CODE OF AUSTRALIA 2022 & HOUSING PROVISIONS STANDARD 2022.
- PART 11.3.5 OF THE NCC VOLUME 2, AMENDMENT 1 - BUILDING CODE OF AUSTRALIA 2022 & HOUSING PROVISIONS STANDARD 2022.
- AS 1170.1-2002 – BALUSTRADEINSTALLATION

PROTECTION OF OPENABLE WINDOW

PART 11.3.7 AND 11.3.8 OF THE NCC VOLUME 2, AMENDMENT 1 - BUILDING CODE OF AUSTRALIA 2022 & HOUSING PROVISIONS STANDARD 2022.

ENERGY EFFICIENCY


- PART 13 OF THE NCC VOLUME 2, AMENDMENT 1 - BUILDING CODE OF AUSTRALIA 2022 & HOUSING PROVISIONS STANDARD 2022 & BASIX CERTIFICATE.

HEATING APPLIANCES, FIREPLACES, CHIMNEYS AND FLUES

- PART 12.4 OF THE NCC VOLUME 2, AMENDMENT 1 - BUILDING CODE OF AUSTRALIA 2022 & HOUSING PROVISIONS STANDARD 2022.

MECHANICAL VENTILATION

- EXHAUST FROM A BATHROOM, SANITARY COMPARTMENT TO DISCHARGE DIRECTLY TO OUTDOOR AIR WITH MINIMUM FLOW RATE OF 25L/S & MAKE-UP AIR VIA OPENINGS TO AN ADJACENT ROOM WITH A FREE AREA OF 14,000 MM^2. THIS EXHAUST SYSTEM MUST BE INTERLOCKED WITH LIGHT SWITCH AND INCLUDE RUN-ON TIMER SO THAT THE EXHAUST SYSTEM CONTINUES TO OPERATE FOR 10 MINUTES AFTER THE LIGHT SWITCH IS OFF.
- ANY INSTALLED - KITCHEN RANGEHOOD EXHAUST TO DISCHARGE DIRECTLY OR VIA DUCT TO OUTDOOR AIR WITH MINIMUM FLOW RATE OF 40L/S & MAKE-UP AIR VIA OPENINGS TO AN ADJACENT ROOM WITH A FREE AREA OF 14,000 MM^2.
- LAUNDRY EXHAUST TO DISCHARGE DIRECTLY OR VIA DUCT TO OUTDOOR AIR WITH MINIMUM FLOW RATE OF 40L/S & MAKE-UP AIR VIA OPENINGS TO AN ADJACENT ROOM WITH A FREE AREA OF 14,000 MM^2.

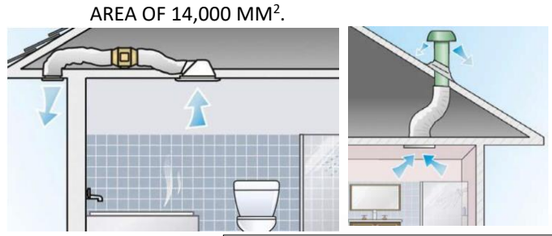

CC ISSUE

REV	DATE	DESCRIPTION	BY
1	28-04-2026	Revision 1	

THIS DRAWING IS THE EXCLUSIVE PROPERTY OF THE DEVELOPER & THE REPRODUCTION OF ANY PART WITHOUT THE PRIOR WRITTEN CONSENT OF THE DEVELOPER IS A VIOLATION OF APPLICABLE LAWS. IN NO EVENT SHALL THE DEVELOPER BE HELD LIABLE FOR SPECIAL COLLATERAL, INCIDENTAL OR CONSEQUENTIAL LIABILITY IN CONNECTION WITH THE USE OF THIS DIGITAL DATA ONCE RELEASED FROM THE DEVELOPER'S OFFICE. THIS DRAWING IS TO BE READ & UNDERSTOOD IN CONJUNCTION WITH THE STRUCTURAL, MECHANICAL, ELECTRICAL & / OR ANY OTHER CONSULTANT'S DOCUMENTATION AS MAY BE APPLICABLE TO THE PROJECT PRIOR TO THE START OF ANY WORKS AND FOR ITS DURATION.

RUBY HOMES

PROJECT:
52 DRINKWATER AVENUE
LOT 42 52 DRINKWATER AVENUE ROUSE HILL

DRAWING TITLE:
GENERAL NOTES A

NORTH:

LOT NO:	DATE:	SCALE:	DRAWING No:	REV:
42	22-05-2024	1 : 2	CC.02A	1
DRAWN BY: AS	CHECKED BY: RH			ISSUED BY:
DRAFTED BY: SL	CLIENT NAME: Owner			

A3

TERMITE SHEET

- TERMITE SHEET EXTENDS THROUGH THE ENTIRE MASONRY LEAF AND **IS VISIBLE AT THE FINISHED FACE OF THE WALL.**


PARAGON
Paragon Building Certifiers Pty Ltd
RBC00045
Registered Certifier
APPROVED
Reference: 260258/01
Date: 10/06/2026



FIGURE 5.5 (in part) TYPICAL SHEET INSTALLATION TO EXTERNAL WALL WITH CONCRETE FLOOR SLAB


OVERFLOW TO BALCONY:

- SURFACE DRAIN & OVERFLOW TO BALCONY

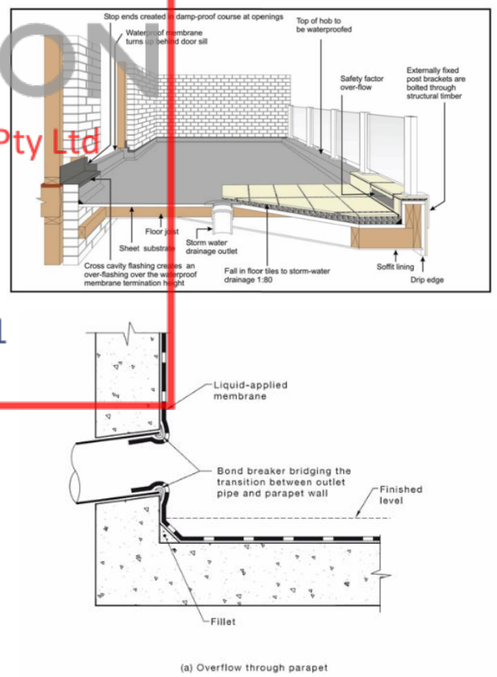

DPC FOR BRICKS

DAMP-PROOF COURSE (DPC) TO EXTENDS THROUGH THE ENTIRE MASONRY LEAF AND **NEED TO BE VISIBLE AT THE FINISHED FACE OF THE WALL FROM OUTSIDE**

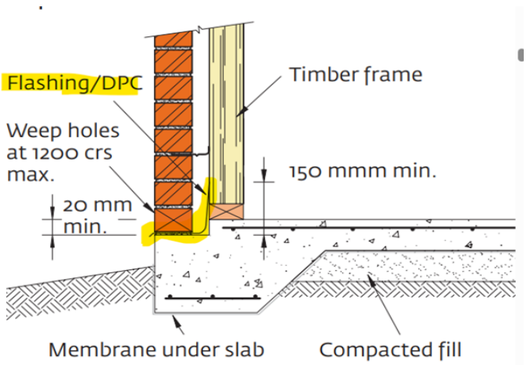

WATERPROOFING

FALL TO FLOOR WASTE TO BE **MINIMUM 1:80 TO MAXIMUM 1:50**

Figure 10.2.29: Typical membrane termination at drainage outlet



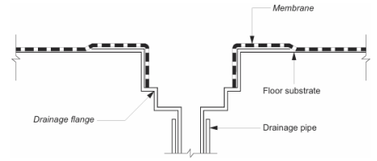


Figure 10.2.24: Typical bathroom door details for whole bathroom waterproofing

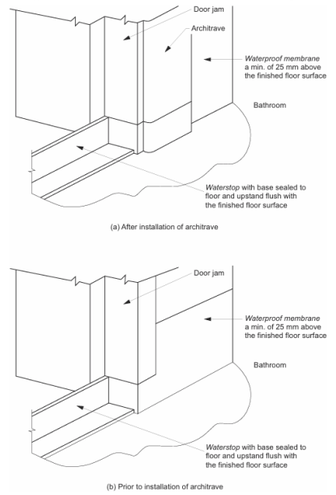


ENCLOSED SHOWER AREA

Figure 10.2.17: Typical hobless construction

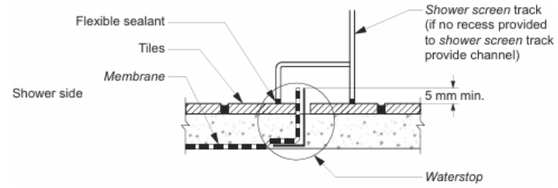



Extent of treatment for shower areas — concrete compressed fibre-cement and fibre-cement sheet floors

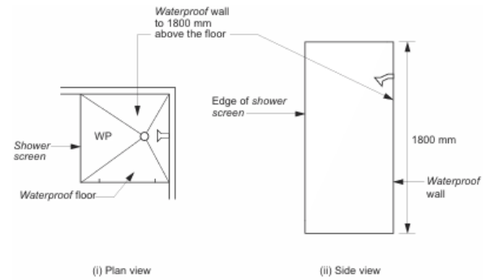

BASIN & BATHTUB:

Figure 10.2.5: Bath and vessel abutting wall — areas to be protected

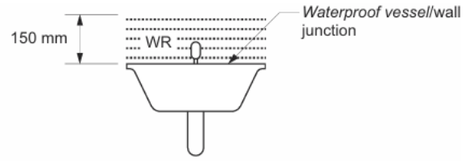

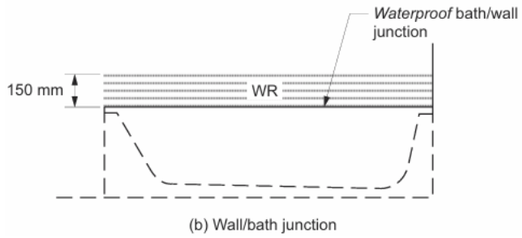

CC ISSUE

REV	DATE	DESCRIPTION	BY
1	28-04-2026	Revision 1	

THIS DRAWING IS THE EXCLUSIVE PROPERTY OF THE DEVELOPER & THE REPRODUCTION OF ANY PART WITHOUT THE PRIOR WRITTEN CONSENT OF THE DEVELOPER IS A VIOLATION OF APPLICABLE LAWS. IN NO EVENT SHALL THE DEVELOPER BE HELD LIABLE FOR SPECIAL, COLLATERAL, INCIDENTAL OR CONSEQUENTIAL LIABILITY IN CONNECTION WITH THE USE OF THIS DIGITAL DATA ONCE RELEASED FROM THE DEVELOPER'S OFFICE. THIS DRAWING IS TO BE READ & UNDERSTOOD IN CONJUNCTION WITH THE STRUCTURAL, MECHANICAL, ELECTRICAL & / OR ANY OTHER CONSULTANT'S DOCUMENTATION AS MAY BE APPLICABLE TO THE PROJECT PRIOR TO THE START OF ANY WORKS AND FOR ITS DURATION.

RUBY HOMES


PROJECT:
52 DRINKWATER AVENUE
LOT 42 52 DRINKWATER AVENUE ROUSE HILL

DRAWING TITLE:
GENERAL NOTES B

NORTH:

LOT NO:	DATE:	SCALE:	DRAWING No:	REV:
42	22-05-2024	1 : 2	CC.02B	1
DRAWN BY: AS	CHECKED BY: RH			ISSUED BY:
DRAFTED BY: SL	CLIENT NAME: Owner			

A3

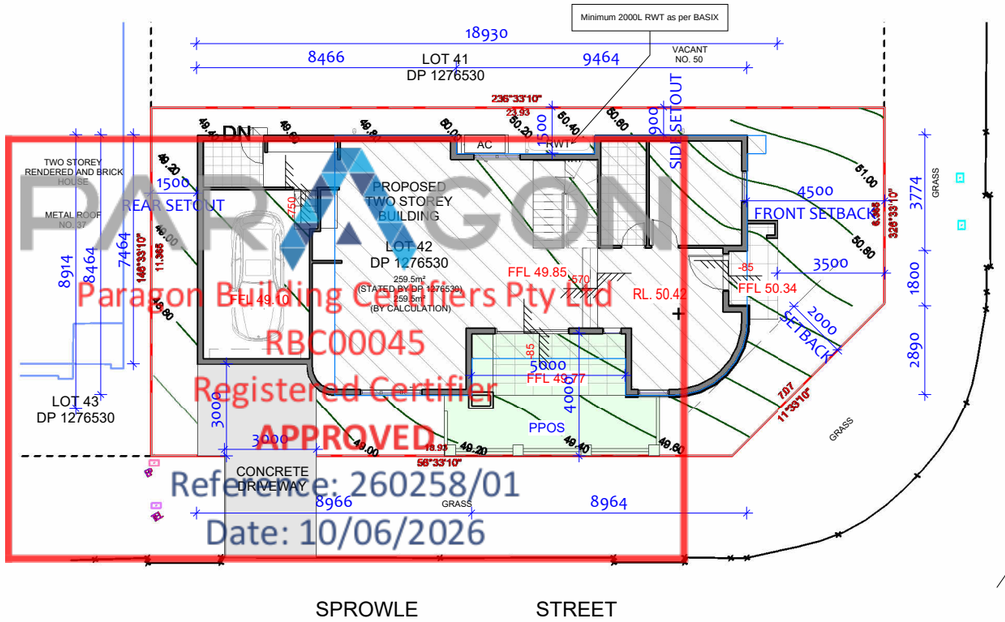

PARAGON
Paragon Building Certifiers Pty Ltd
RBC00045
Registered Certifier
APPROVED
Reference: 260258/01
Date: 10/06/2026

CC - SITE PLAN


1 : 200

LEGENDS

- GROUND FLOOR
- FIRST FLOOR
- SEWER LINE

Blacktown City Council Growth Centre Precincts
Development Control Plan 2010

DESCRIPTION		COMPLIANCE		COMMENT
ELEMENT	CODE CONTROL	REQUIREMNT	PROPOSED	
LAND ZONE	R2 - Low Density Residential			
LOT NO	LOT 42			
LOT AREA	259.5 m2			
HEIGHT	storeys maximum (3rd storey subject to clause 4.2.5 (1))		8.5m	YES
FRONT SETBACK	4.5m to building facade line; 3.5m to building facade fronting open space or drainage land		4.5 m	YES
REAR SET BACK (MIN.)	GROUND FLOOR	-	1.5m	YES
	FIRST FLOOR	6m	6 m	
SIDE SET BACK (MIN.)	GROUND FLOOR	2/0.9m	2/0.9m	YES
	FIRST FLOOR	2/0.9m	2/0.9m	
SITE COVERAGE	GROUND FLOOR	50%	103sqm/39.6% Lot area	YES
	FIRST FLOOR	40%	89sqm/34.3.% Lot area	
PRIVATE OPEN SPACE	Minimum 20m² with minimum dimension of 4.0m.		24 m2	YES
LANDSCAPE AREA	25 % of TOTAL LAND AREA	64.8 m2	81.17 m2	YES

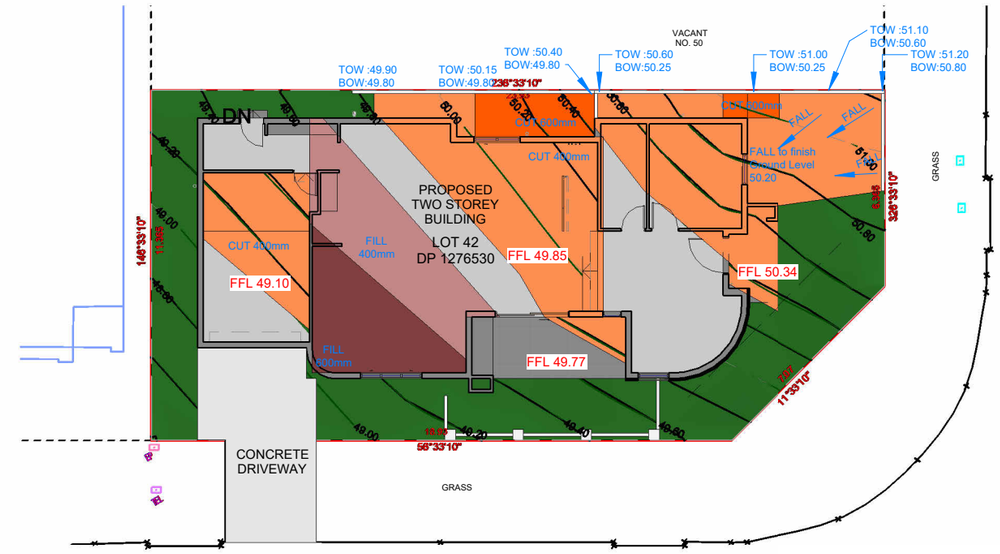

CC - CUT AND FILL

1 : 200

LEGENDS

- CUT (100-400) mm
- CUT (400-600) mm
- FILL (100-400) mm
- FILL (400-600) mm

Area Schedule (Rentable)

Name	Area

Ground Floor

GARAGE	20 m²
GFA	102 m²
PORCH	4 m²
ALFRESCO	10 m²
Ground Floor: 4	135 m²

Level 1

FFA	89 m²
VOID	6 m²
BALCONY2	6 m²
BALCONY	3 m²
Level 1: 4	103 m²
Grand total: 8	239 m²

SITE COVERAGE

GROUND FLOOR
Required: Max.129.7sqm/50% Lot area
Proposed:103sqm/39.6% Lot area

FIRST FLOOR
Required: Max. 103.7sqm/40% Lot area
Proposed: 89sqm/34.3% Lot area

LANDSCAPE
Required: Max.210.8sqm/30% Lot area
Proposed: 81.17sqm,31.2%

POS
Required: 20sqm
Proposed: 24sqm

CC ISSUE

REV	DATE	DESCRIPTION	BY
1	28-04-2026	Revision 1	

THIS DRAWING IS THE EXCLUSIVE PROPERTY OF THE DEVELOPER & THE REPRODUCTION OF ANY PART WITHOUT THE PRIOR WRITTEN CONSENT OF THE DEVELOPER IS A VIOLATION OF APPLICABLE LAWS. IN NO EVENT SHALL THE DEVELOPER BE HELD LIABLE FOR SPECIAL COLLATERAL, INCIDENTAL OR CONSEQUENTIAL LIABILITY IN CONNECTION WITH THE USE OF THIS DIGITAL DATA ONCE RELEASED FROM THE DEVELOPER'S OFFICE. THIS DRAWING IS TO BE READ & UNDERSTOOD IN CONJUNCTION WITH THE STRUCTURAL, MECHANICAL, ELECTRICAL & / OR ANY OTHER CONSULTANT'S DOCUMENTATION AS MAY BE APPLICABLE TO THE PROJECT PRIOR TO THE START OF ANY WORKS AND FOR ITS DURATION.

RUBY HOMES


PROJECT:
52 DRINKWATER AVENUE
LOT 42 52 DRINKWATER AVENUE ROUSE HILL

DRAWING TITLE:
LOCATION PLAN AND SITE PLAN

NORTH:

LOT NO: 42	DATE: 22-05-2024	SCALE: As indicated	DRAWING No: CC.03	REV: 1
DRAWN BY: AS	CHECKED BY: RH			ISSUED BY:
DRAFTED BY: SL	CLIENT NAME: Owner			

A3

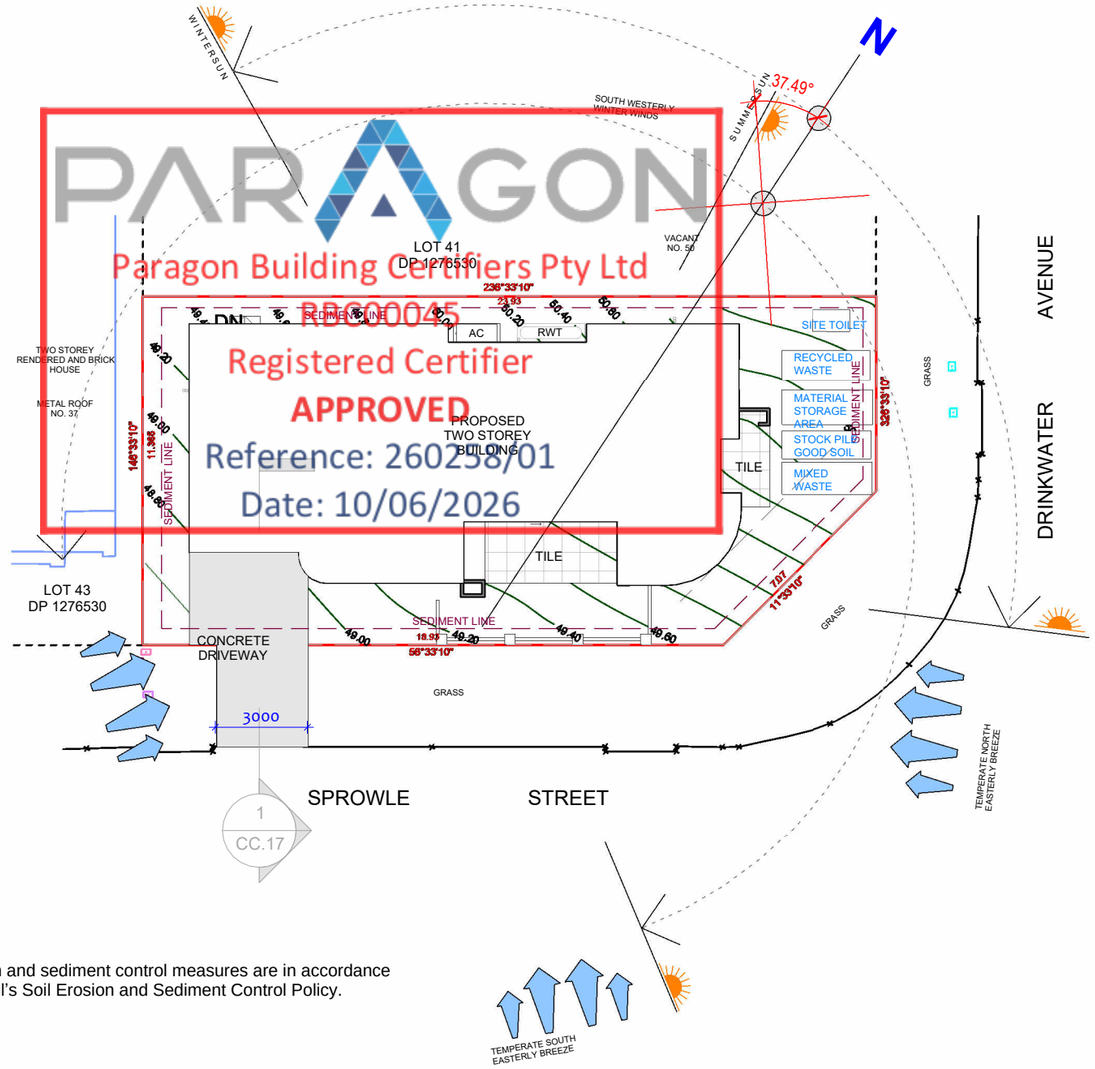

PARAGON
Paragon Building Certifiers Pty Ltd
BDC0045
Registered Certifier
APPROVED
Reference: 260258/01
Date: 10/06/2026

Soil erosion and sediment control measures are in accordance with Council's Soil Erosion and Sediment Control Policy.

1 CC - SITE ANALYSIS AND SEDIMENT CONTROL PLAN

1 : 200

TEMPORARY 1.8M HIGH WIRE ML FENCE WITH DUSTPROOF MESH APPLIED TO FULL HEIGHTTO BOUNDARIES AS REQUIRED

LOCATION OF WASTE BINS

SEDIMENT FENCE AS REQUIRED

GRAVEL ACCESS

SITE ACCESS AREA TO BE USED FOR WASHDOWN AREA

FOOTPATH CLEAN AND CLEAR AT ALL TIMES

LOCATION OF STOCKPILE MATERIAL
MATERIAL STORAGE AREA
TEMPORARY TOILETS
INSTALL TEMPORARY SEDIMENT BARRIERS TO ALL INLET PITS LIKELY TO COLLECT SILT LADDEN WATER, TO COUNCILS'S REQUIREMENTS.

SD 5-7 STABILISED SITE ACCESS

1) STRIP TOPSOIL AND LEVEL SITE.
2) COMPACT SUBGRADE.
3) COVER AREA WITH GEOTEXILE.
4) CONSTRUCT 200 mm THICK PAD OVER GEOTEXILE USING ROADBASE OR 30 mm AGGREGATE. Min 15 m LONG OR TO BUILDING ALIGNMENT. Min 3 m WIDE.
5) CONSTRUCT HUMP IMMEDIATELY WITHIN BOUNDARY TO DIVERT WATER TO A SEDIMENT FENCE OR OTHER SEDIMENT TRAP.

SD 6-9 GEOTEXTILE INLET FILTER

1) FABRICATE A SEDIMENT BARRIER MADE FROM GEOTEXILE. REFER SD6-7 FOR DETAILS.
2) SUPPORT GEOTEXILE WITH MESH TIED TO POSTS AT 1 m Ctrs.
3) DO NOT COVER INLET WITH GEOTEXILE.

SITE WORKS NOTES


1.ORIGIN OF LEVELS PROVIDED BY SURVEYIOR

2.THE BUILDER SHALL VERIFY ALL DIMENSIONS AND EXISTING LEVELS ON SITE PERIOR TO THE COMMENCEMENT OF WORK AND ANY DISCREPANNCIES SHALL BE REPORTED TO THE SURVEYOR / ENGINEER .

3. TOPSOIL SHALL BE STRIPPED FROM THE CONSTRUCTUTION AREA AND SOCKPILED ON SITE , TO BE LATER SPREAD OR DISPOSED OFF SITE ,AS DIRECTED BY SUPERVISOR /ENGINEER .


4. ALL TH TRENCH BACKFILL MATERIAL SHAL BE COMPACTED TO THE SAME DENSITY AS THE ADJACENT MATERIAL.

5. ALL SERVICE TRENCHES UNDER VEHICULAR PAVEMENTS SHALL BE BACKFILLED WITH SAND OR APPROVED GRANULAR MATERIALS. TO THE UNDERSIDE OF THE PAVEMENT, AND COMPACTED TO 98%STANDARD MAXIMUM DRY DENSITY ,IN ACCORDANCE WITH AS 1289E1.1.

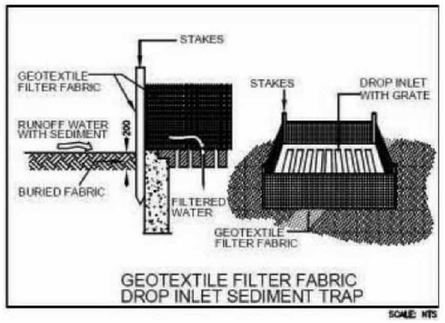


GEOTEXTILE FILTER FABRIC DROP INLET SEDIMENT TRAP

SCALE: NTS

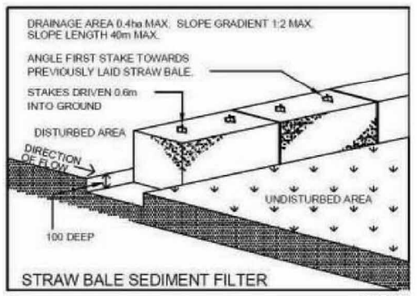


STRAW BALE SEDIMENT FILTER

SCALE: NTS

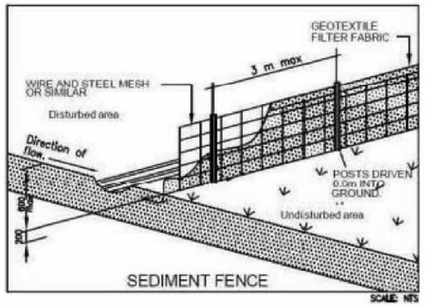

SEDIMENT FENCE

SCALE: NTS

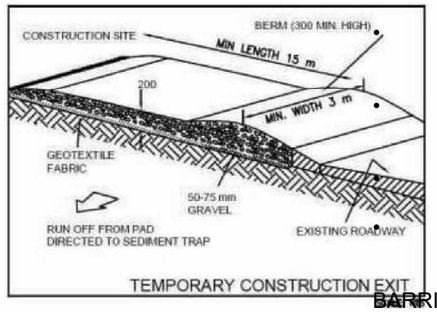

TEMPORARY CONSTRUCTION EXIT

SCALE: NTS

SEDIMENT AND EROSION NOTES:

- THIS PLAN TO BE READ IN CONJUNCTION WITH SEDIMENT AND EROSION CONTROL DETAILS AS ATTACHED.
- THE CONTRACTOR SHALL IMPLEMENT ALL SOIL EROSION AND SEDIMENT CONTROL MEASURES AS NECESSARY AND TO THE SATISFACTION OF COUNCIL PRIOR TO THE COMMENCEMENT AND DURING CONSTRUCTION.NO DISTURBANCE TO THE SITE SHALL BE PERMITTED OTHER THAN IN THE IMMEDIATE AREA OF THE WORK AND NO MATERIAL SHALL BE REMOVED FROM THE SITE WITHOUT COUNCIL'S APPROVAL.ALL SEDIMENTAND EROSION CONTROL DEVICES TO BE INSTALLED AND MAINTAINED IN ACCORDANCE WITH STANDARDS OUTLINED IN NSW DEPARTMENT OF HOUSING "MANAGING URBAN STORMWATER-SOILS AND CONSTRUCTIONS".
- TOPSOIL SHALL BE STRIPPED AND STOCKPILED OUTSIDE HAZARD AREAS SUCH AS DRAINAGE LINES.THIS TOP SOIL IS TO BE RESPIRED LATER ON AREAS TO BE REVEGETATED AND STABLISED ONLY. (I.E ALL FOOTPATHS,BATTERS,SITE REGARDING AREAS,BASINS AND CATCH DRAINS),TOPSOIL SHALL NOT BE RESPIRED ON ANY OTHER AREAS UNLESS SPECIALLY INSTRUCTED BY THE SUPERIDENT.IF THEY ARE TO REMAIN FOR LONGER THAN ONE MONTH STOCKPILES SHALL BE PROTECTED FROM EROSION BY COVERING THEM WITH A MULCH AND HYDROSEEDING AND,IF NECESSARY,BY LOCATING BANKS OR DRAINS DOWNSTREAM OF A STOCKPILE TO RETARD SILT LADEN RUNOFF.
- THE CONTRACTOR SHALL REGULARLY MAINTAIN ALL SEDIMENT AND EROSION CONTROL DEVICES AND REMOVE ACCUMULATED SILT FROM SUCH DEVICES SUCH THAT MORE THAN 60% OF THEIR CAPACITY LOST.ALL THE SILTS TO BE PLACED OUTSIDE THE LIMIT OF WORKS.THE PERIOD FOR MAINTAINING THESE DEVICES SHALL BE AT LEAST UNTIL ALL DISTURBED AREAS ARE REVEGETATED AND FURTHER AS MAY BE DIRECTED BY THE SUPERINTENDENT OR COUNCIL.
- LAY TURF STRIP (MIN 300 mm WIDE) ON 100 mm TOPSOIL WITH 1.0 m LONG RETURNS EVERY 6.0m BEHIND ALL KERB AT THE TOP OF ALL BATTERS AND AROUND STRUCTURES IMMEDIATELY AFTER BACKFILLING OR FORMATION.
- THE CONTRACTOR SHALL GRASS SEED ALL DISTURBED AREAS WITH AN APPROVED MIX AS SSON AS PRACTICABLE AFTER COMPLETION OF EARTHWORKS AND REGRADING.
- VEHICULAR TRAFFIC SHALL BE CONTROLLED DURING CONSTRUCION CONFINNG ACCESS WHERE POSSIBLE TO NOMINATED STABLISED ACCESS POINTS.
- WHEN ANY DEVICES ARE TO BE HANDED OVER TO COUNCIL,THEY SHALL BE IN CLEAN AND STABLE CONDITION.
- THE CONTRACTOR SHALL IMPLEMENT DUST CONTROL BY REGULAR WETTING DOWN(BUT NOT SATURATING) DISTURBED AREA.
- PROVIDE AND MAINTAIN SILT TRAPS AROUND ALL SURFACE INLET PITS UNTL CATCHMENT IS REVEGETATED OR PAVED.
- REVEGETATE ALL TRENCHES IMMEDIATELY UPON COMPLETION OF BACKFILLING.
- ALL DRAINAGE PIPE INLETS TO BE CAPPED UNTIL:
  A) DOWNPIPES CONNECTED
  B) PITS CONSTRUCTED & PROTECTED WITH SILT BARRIER

CC ISSUE

REV	DATE	DESCRIPTION	BY
1	28-04-2026	Revision 1	

THIS DRAWING IS THE EXCLUSIVE PROPERTY OF THE DEVELOPER & THE REPRODUCTION OF ANY PART WITHOUT THE PRIOR WRITTEN CONSENT OF THE DEVELOPER IS A VIOLATION OF APPLICABLE LAWS. IN NO EVENT SHALL THE DEVELOPER BE HELD LIABLE FOR SPECIAL COLLATERAL, INCIDENTAL OR CONSEQUENTIAL LIABILITY IN CONNECTION WITH THE USE OF THIS DIGITAL DATA ONCE RELEASED FROM THE DEVELOPER'S OFFICE. THIS DRAWING IS TO BE READ & UNDERSTOOD IN CONJUNCTION WITH THE STRUCTURAL, MECHANICAL, ELECTRICAL & / OR ANY OTHER CONSULTANT'S DOCUMENTATION AS MAY BE APPLICABLE TO THE PROJECT PRIOR TO THE START OF ANY WORKS AND FOR ITS DURATION.

RUBY HOMES

PROJECT:
52 DRINKWATER AVENUE
LOT 42 52 DRINKWATER AVENUE ROUSE HILL

DRAWING TITLE:
SITE ANALYSIS AND SEDIMENT CONTROL


NORTH:

LOT NO:	DATE:	SCALE:	DRAWING No:	REV:
42	22-05-2024	As indicated	CC.04	1
DRAWN BY: AS	CHECKED BY: RH			ISSUED BY:
DRAFTED BY: SL	CLIENT NAME: Owner			

A3

IMPORTANT NOTES:
ALL DIMENSIONS AND NOTES ON ALL PLANS MUST BE CHECKED AND VERIFIED BY BUILDERS AND OWNER PRIOR TO COMMENCEMENT OF ANY BUILDING WORKS. TO CLARIFY AND CONFIRM WITH CONSTRUCTION COMPANY FOR DISCREPANCIES ON ALL DOCUMENTS AND PLANS PROVIDED FOR CONSTRUCTION.ANY WORK INDICATED ON THE PLAN BUT NOT IN THE SPECIFICATION BUT WHICH IS NECESSARY AS PART OF THE CONTRACT,VARIATION TO PLANS,SPECIFICATIONS MAY NOT BE MADE WITHOUT THE WRITTEN CONSENT OF OWNER.IT IS THE RESPONSIBILITY OF THE BUILDER/END USER TO VERIFY PLANS AND SPECIFICATIONS AS TO THEIR ACCURACY AND COMPLY CURRENT BCA AND AUSTRALIAN STANDARDS.
WINDOWS TO COMPLY WITH 3.9.3.5 OF THE BCA.

PARAGON
Paragon Building Certifiers Pty Ltd
RBC00045
Registered Certifier
APPROVED
Reference: 260258/01
Date: 11/06/2026

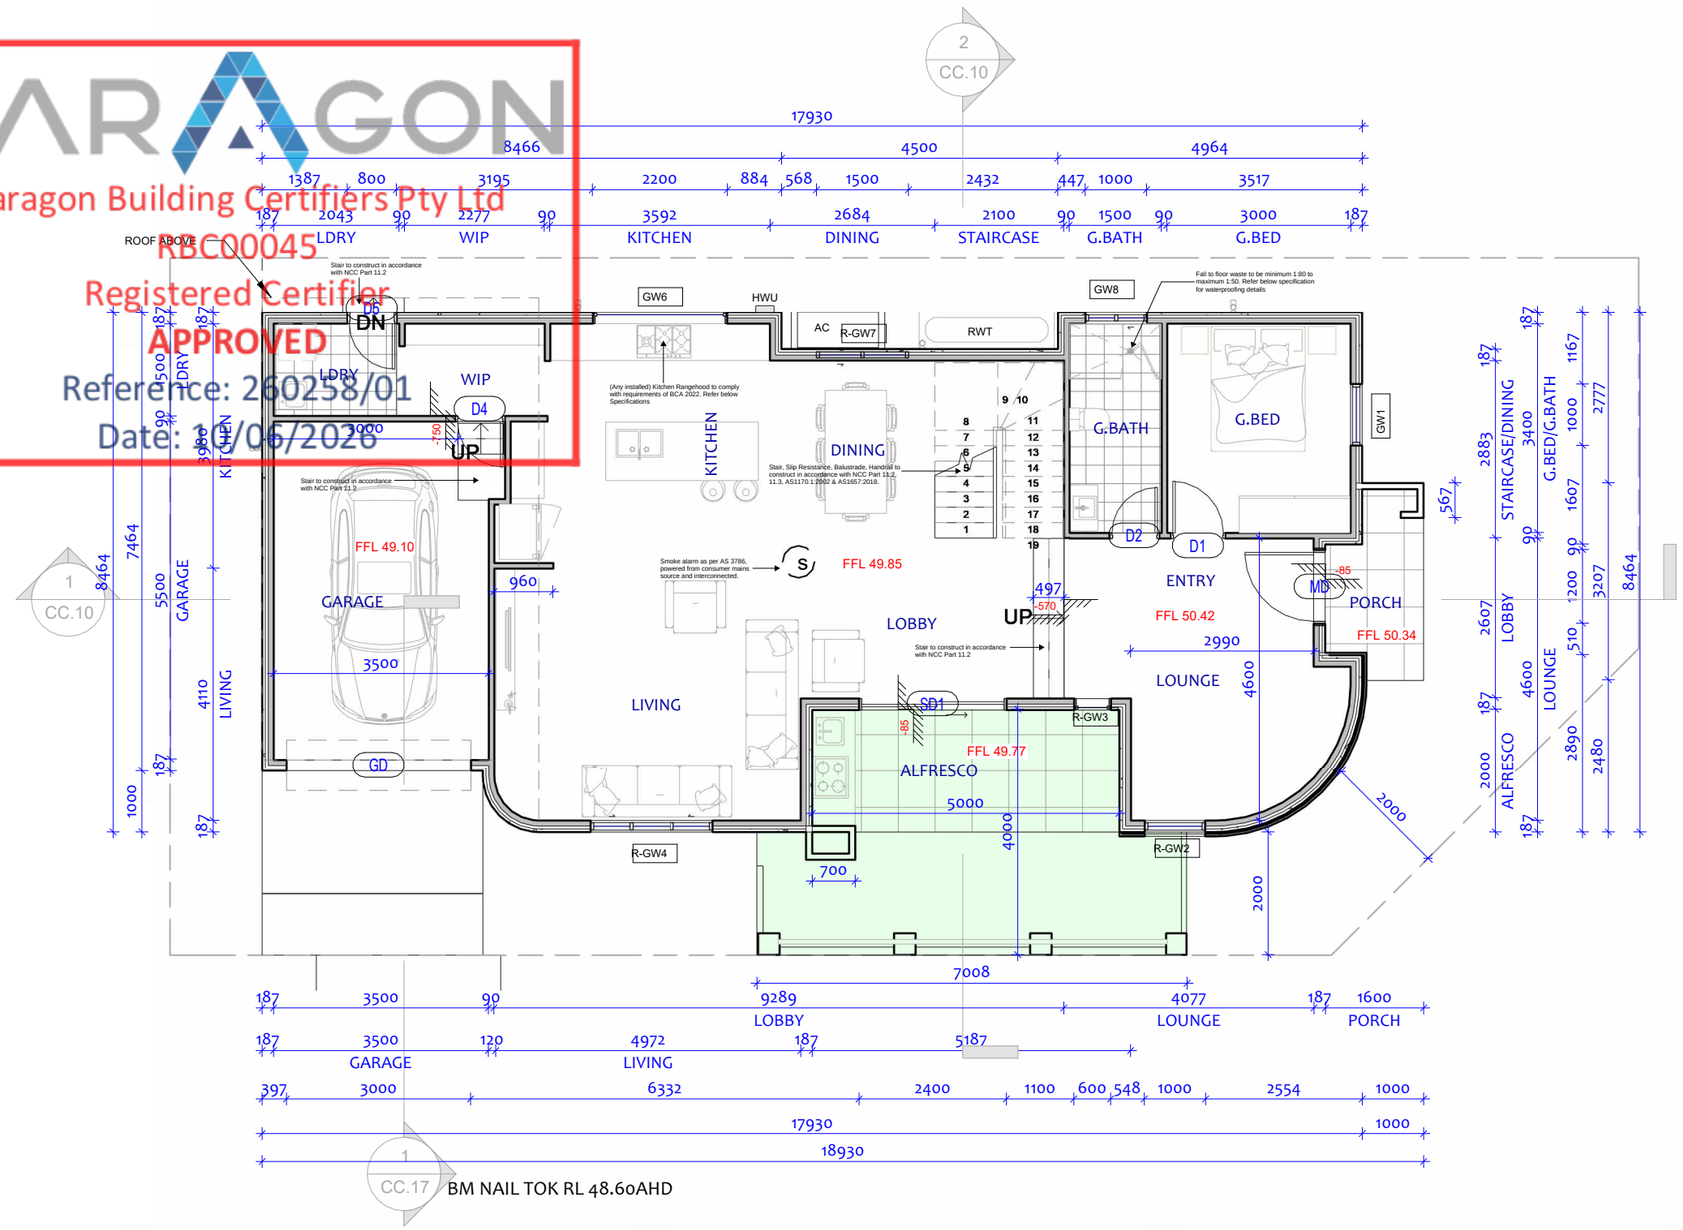

1 Ground Floor
1 : 100

Waterproofing work to be as per Part 10.2 of the ABCB Housing Provisions Standard 2022

REV	DATE	DESCRIPTION	BY
1	28-04-2026	Revision 1	

THIS DRAWING IS THE EXCLUSIVE PROPERTY OF THE DEVELOPER & THE REPRODUCTION OF ANY PART WITHOUT THE PRIOR WRITTEN CONSENT OF THE DEVELOPER IS A VIOLATION OF APPLICABLE LAWS. IN NO EVENT SHALL THE DEVELOPER BE HELD LIABLE FOR SPECIAL COLLATERAL, INCIDENTAL OR CONSEQUENTIAL LIABILITY IN CONNECTION WITH THE USE OF THIS DIGITAL DATA ONCE RELEASED FROM THE DEVELOPER'S OFFICE. THIS DRAWING IS TO BE READ & UNDERSTOOD IN CONJUNCTION WITH THE STRUCTURAL, MECHANICAL, ELECTRICAL & / OR ANY OTHER CONSULTANT'S DOCUMENTATION AS MAY BE APPLICABLE TO THE PROJECT PRIOR TO THE START OF ANY WORKS AND FOR ITS DURATION.

RUBY HOMES

PROJECT:
52 DRINKWATER AVENUE
LOT 42 52 DRINKWATER AVENUE ROUSE HILL

DRAWING TITLE:
GROUND FLOOR PLAN

NORTH:


CC ISSUE

LOT NO:	DATE:	SCALE:	DRAWING No:	REV:
42	22-05-2024	1 : 100	CC.05	1
DRAWN BY: AS	CHECKED BY: RH			ISSUED BY:
DRAFTED BY: SL	CLIENT NAME: Owner			

A3

IMPORTANT NOTES:
ALL DIMENSIONS AND NOTES ON ALL PLANS MUST BE CHECKED AND VERIFIED BY BUILDERS AND OWNER PRIOR TO COMMENCEMENT OF ANY BUILDING WORKS. TO CLARIFY AND CONFIRM WITH CONSTRUCTION COMPANY FOR DISCREPANCIES ON ALL DOCUMENTS AND PLANS PROVIDED FOR CONSTRUCTION.ANY WORK INDICATED ON THE PLAN BUT NOT IN THE SPECIFICATION BUT WHICH IS NECESSARY AS PART OF THE CONTRACT,VARIATION TO PLANS,SPECIFICATIONS MAY NOT BE MADE WITHOUT THE WRITTEN CONSENT OF OWNER.IT IS THE RESPONSIBILITY OF THE BUILDER/END USER TO VERIFY PLANS AND SPECIFICATIONS AS TO THEIR ACCURACY AND COMPLY CURRENT BCA AND AUSTRALIAN STANDARDS.
WINDOWS TO COMPLY WITH 3.9.3.5 OF THE BCA.

PARAGON
Paragon Building Certifiers Pty Ltd
RBC00045
Registered Certifier
APPROVED
Reference: 260258/01
Date: 10/06/2026

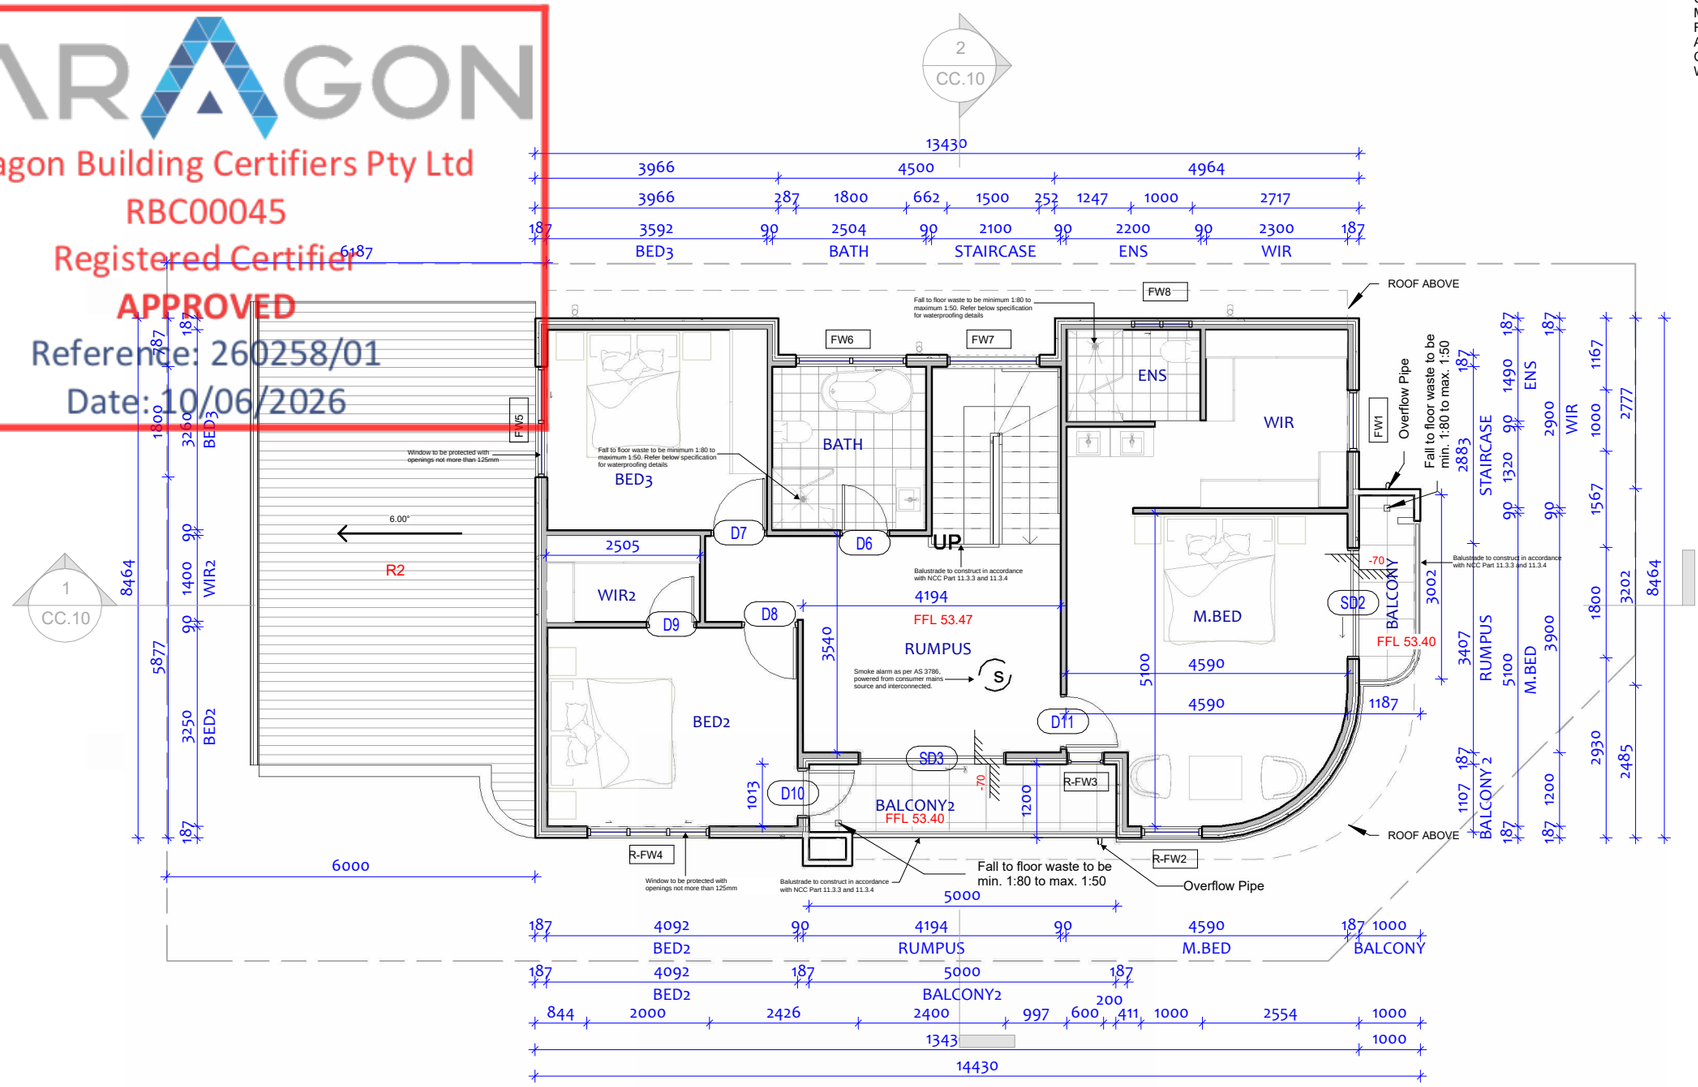

1 Level 1
1 : 100

Waterproofing work to be as per Part 10.2 of the ABCB Housing Provisions Standard 2022

CC ISSUE

REV	DATE	DESCRIPTION	BY
1	28-04-2026	Revision 1	

THIS DRAWING IS THE EXCLUSIVE PROPERTY OF THE DEVELOPER & THE REPRODUCTION OF ANY PART WITHOUT THE PRIOR WRITTEN CONSENT OF THE DEVELOPER IS A VIOLATION OF APPLICABLE LAWS. IN NO EVENT SHALL THE DEVELOPER BE HELD LIABLE FOR SPECIAL COLLATERAL, INCIDENTAL OR CONSEQUENTIAL LIABILITY IN CONNECTION WITH THE USE OF THIS DIGITAL DATA ONCE RELEASED FROM THE DEVELOPER'S OFFICE. THIS DRAWING IS TO BE READ & UNDERSTOOD IN CONJUNCTION WITH THE STRUCTURAL, MECHANICAL, ELECTRICAL & / OR ANY OTHER CONSULTANT'S DOCUMENTATION AS MAY BE APPLICABLE TO THE PROJECT PRIOR TO THE START OF ANY WORKS AND FOR ITS DURATION.

RUBY HOMES

PROJECT:
52 DRINKWATER AVENUE
LOT 42 52 DRINKWATER AVENUE ROUSE HILL

DRAWING TITLE:
FIRST FLOOR LEVEL

NORTH:


LOT NO:	DATE:	SCALE:	DRAWING No:	REV:
42	22-05-2024	1 : 100	CC.06	1
DRAWN BY: AS	CHECKED BY: RH			ISSUED BY:
DRAFTED BY: SL	CLIENT NAME: Owner			

A3

IMPORTANT NOTES:
ALL DIMENSIONS AND NOTES ON ALL PLANS MUST BE CHECKED AND VERIFIED BY BUILDERS AND OWNER PRIOR TO COMMENCEMENT OF ANY BUILDING WORKS. TO CLARIFY AND CONFIRM WITH CONSTRUCTION COMPANY FOR DISCREPANCIES ON ALL DOCUMENTS AND PLANS PROVIDED FOR CONSTRUCTION.ANY WORK INDICATED ON THE PLAN BUT NOT IN THE SPECIFICATION BUT WHICH IS NECESSARY AS PART OF THE CONTRACT,VARIATION TO PLANS,SPECIFICATIONS MAY NOT BE MADE WITHOUT THE WRITTEN CONSENT OF OWNER.IT IS THE RESPONSIBILITY OF THE BUILDER/END USER TO VERIFY PLANS AND SPECIFICATIONS AS TO THEIR ACCURACY AND COMPLY CURRENT BCA AND AUSTRALIAN STANDARDS.
WINDOWS TO COMPLY WITH 3.9.3.5 OF THE BCA.

PARAGON

Paragon Building Certifiers Pty Ltd
RBC00045
Registered Certifier
APPROVED
Reference: 260258/01
Date: 10/06/2026

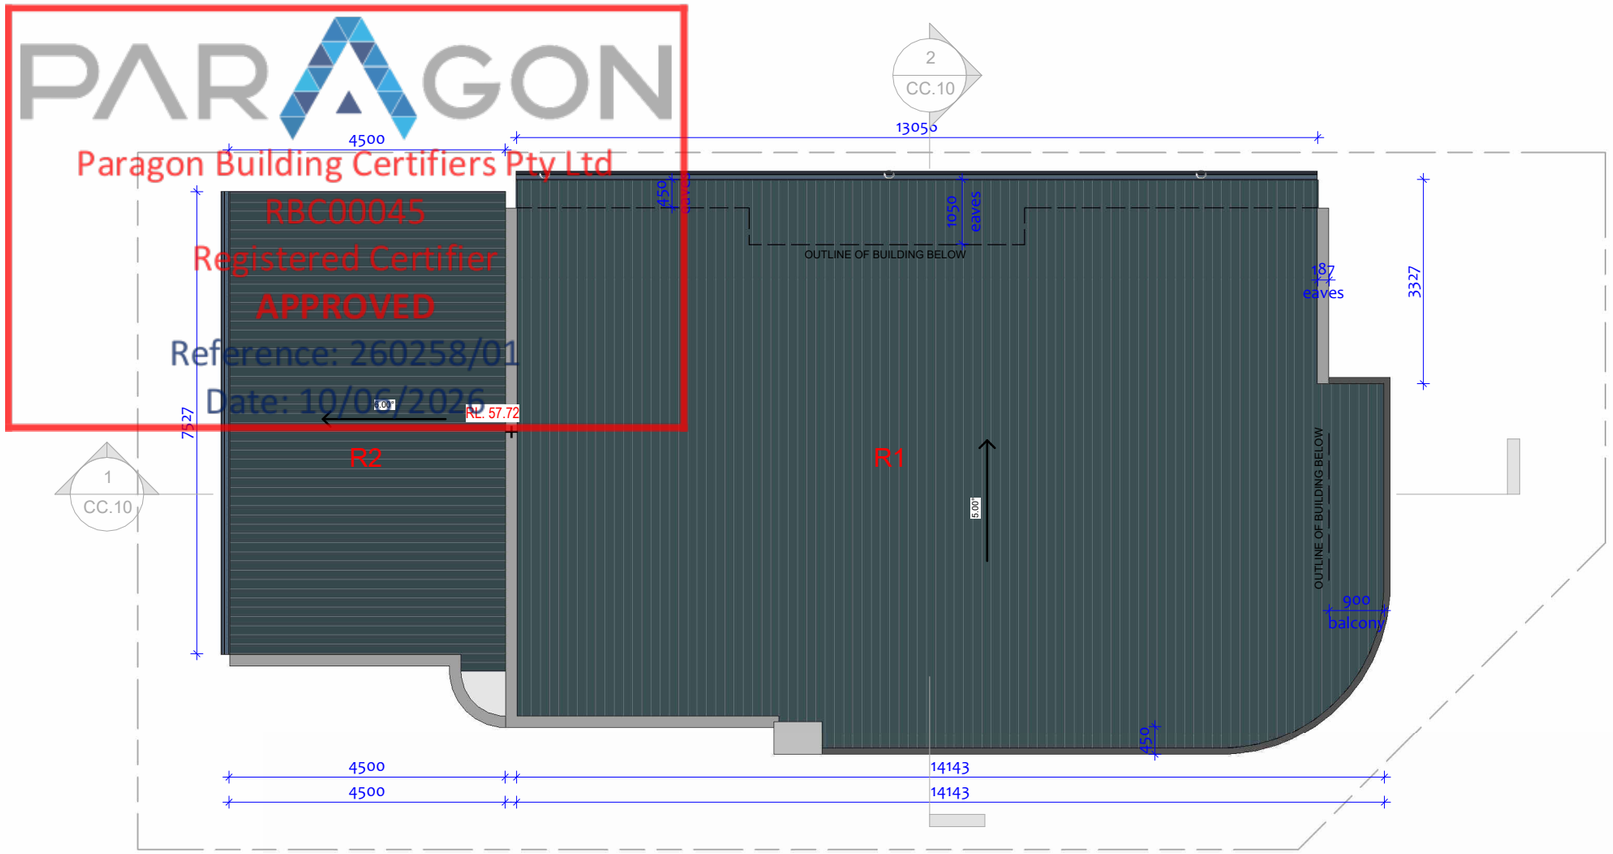

ROOF PLAN
1 : 100

Minimum pitch requirements for metal roofing profiles



Corrugated
Minimum pitch – 5 degrees

Close pitched trapezoidal
Minimum pitch – 2 degrees



Trapezoidal
Minimum pitch – 2 degrees

Concealed fastened
Minimum pitch – 1 degree


VENTILATION OF ROOF SPACES

ROOF SPACE AS PER 10.8.3 1(a) & 1(b)

(i) VENTILATED TO OUTDOOR AIR THROUGH EVENLY DISTRIBUTED OPENINGS IN ACCORDANCE WITH TABLE 10.8.3;

TABLE 10.8.3: ROOF SPACE VENTILATION REQUIREMENTS

ROOF PITCH	VENTILATION OPENINGS
< 10°	25,000 MM2/M PROVIDED AT EACH OF TWO OPPOSING ENDS
≥ 10° AND < 15°	25,000 MM2/M PROVIDED AT THE EAVES AND 5,000 MM2/M AT HIGH LEVEL
≥ 15° AND < 75°	7,000 MM2/M PROVIDED AT THE EAVES AND 5,000 MM2/M AT HIGH LEVEL, PLUS AN ADDITIONAL 18,000 MM2/M AT THE EAVES IF THE ROOF HAS A CATHEDRAL CEILING

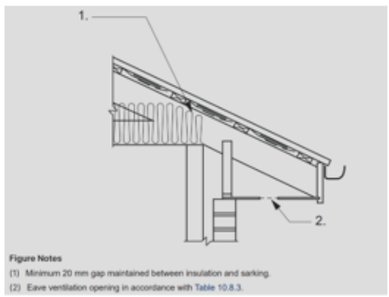

Roof Schedule			
Mark	Base Level	Area	Comments
R1	CEILING LEVEL	124 m²	COLORBOND
R2	Level 1	35 m²	COLORBOND
Grand total: 2		159 m²	

CC ISSUE

REV	DATE	DESCRIPTION	BY
1	28-04-2026	Revision 1	

THIS DRAWING IS THE EXCLUSIVE PROPERTY OF THE DEVELOPER & THE REPRODUCTION OF ANY PART WITHOUT THE PRIOR WRITTEN CONSENT OF THE DEVELOPER IS A VIOLATION OF APPLICABLE LAWS. IN NO EVENT SHALL THE DEVELOPER BE HELD LIABLE FOR SPECIAL, COLLATERAL, INCIDENTAL OR CONSEQUENTIAL LIABILITY IN CONNECTION WITH THE USE OF THIS DIGITAL DATA ONCE RELEASED FROM THE DEVELOPER'S OFFICE. THIS DRAWING IS TO BE READ & UNDERSTOOD IN CONJUNCTION WITH THE STRUCTURAL, MECHANICAL, ELECTRICAL & / OR ANY OTHER CONSULTANT'S DOCUMENTATION AS MAY BE APPLICABLE TO THE PROJECT PRIOR TO THE START OF ANY WORKS AND FOR ITS DURATION.

RUBY HOMES


PROJECT:
52 DRINKWATER AVENUE
LOT 42 52 DRINKWATER AVENUE ROUSE HILL

DRAWING TITLE:
ROOF PLAN

NORTH:


LOT NO:	DATE:	SCALE:	DRAWING No:	REV:
42	22-05-2024	1 : 100	CC.07	1
DRAWN BY: AS	CHECKED BY: RH			ISSUED BY:
DRAFTED BY: SL	CLIENT NAME: Owner			

A3

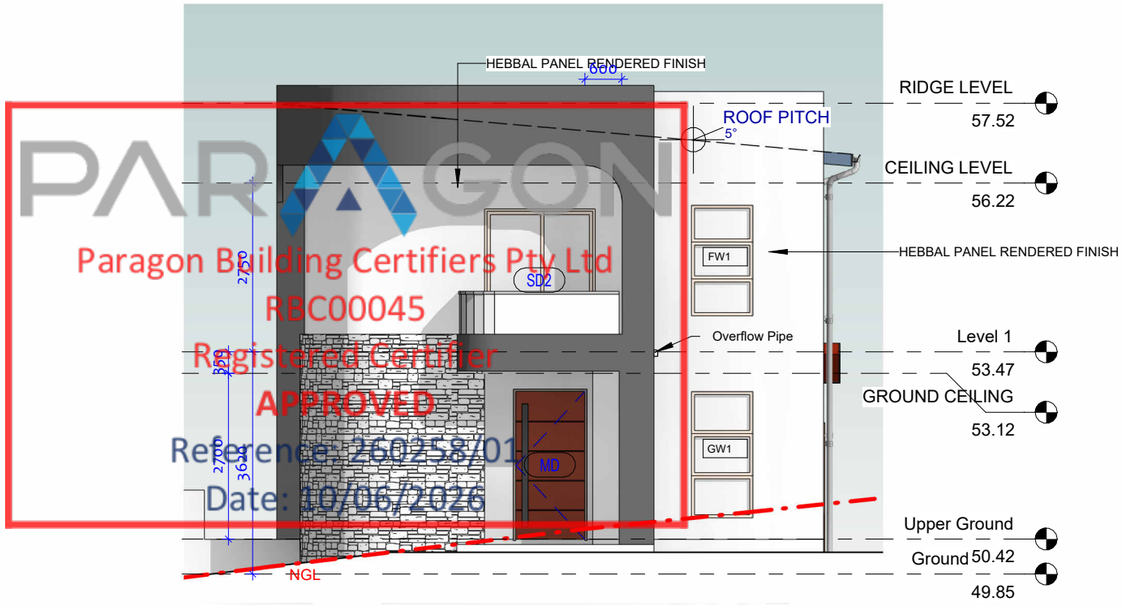

1 NORTH EAST ELEVATION

1 : 100

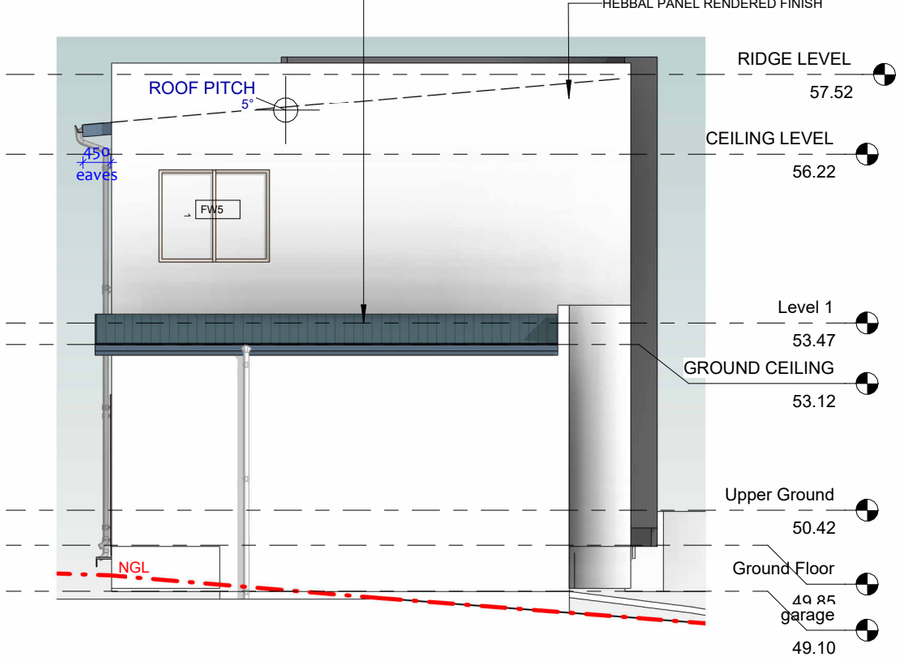

2 SOUTH WEST ELEVATION

1 : 100

PARAGON
Paragon Building Certifiers Pty Ltd
RBC00045
Registered Certifier
APPROVED
Reference: 260258/01
Date: 10/06/2026

Window Schedule 1					
Mark	Height	Width	Sill Height	Head Height	Description
Ground Floor					
GW6	600	2200	900	1500	FIXED
R-GW4	2200	2000	500	2700	SLIDING & FIXED
R-GW7	800	1500	1600	2400	SLIDING
Ground Floor: 3					
Upper Ground					
GW1	2050	1000	350	2400	FIXED
GW8	800	1000	1800	2600	SLIDING
R-GW2	2050	1000	350	2400	FIXED
R-GW3	2050	600	350	2400	FIXED
Upper Ground: 4					
Level 1					
FW1	1800	1000	600	2400	FIXED
FW5	1500	1800	1000	2500	SLIDING
FW6	1400	1800	1000	2400	SLIDING
FW7	2400	1500	0	2400	FIXED
FW8	800	1000	1600	2400	SLIDING
R-FW2	2050	1000	350	2400	FIXED
R-FW3	2050	600	350	2400	FIXED
R-FW4	2200	2000	500	2700	SLIDING & FIXED
Level 1: 8					

Door Schedule 1				
Mark	Height	Width	Count	Description
garage				
GD	2500	3000	1	GARAGE DOOR
garage: 1				
Ground Floor				
D1	2340	820	1	SOLID FLUSH DOOR
D5	2340	720	1	SOLID FLUSH DOOR
D2	2340	720	1	SOLID FLUSH DOOR
SD1	2300	2400	1	SLIDING DOOR
D4	2340	720	1	SOLID FLUSH DOOR
Ground Floor: 5				
Upper Ground				
MD	2400	1120	1	SOLID CORE DOOR
Upper Ground: 1				
Level 1				
D7	2340	820	1	SOLID FLUSH DOOR
D6	2340	720	1	SOLID FLUSH DOOR
D9	2340	720	1	SOLID FLUSH DOOR
SD3	2300	2400	1	SLIDING DOOR
D11	2340	820	1	SOLID FLUSH DOOR
D8	2340	820	1	SOLID FLUSH DOOR
SD2	2300	1800	1	SLIDING DOOR
D10	2340	720	1	SOLID FLUSH DOOR
Level 1: 8				

CC ISSUE

REV	DATE	DESCRIPTION	BY
1	28-04-2026	Revision 1	

THIS DRAWING IS THE EXCLUSIVE PROPERTY OF THE DEVELOPER & THE REPRODUCTION OF ANY PART WITHOUT THE PRIOR WRITTEN CONSENT OF THE DEVELOPER IS A VIOLATION OF APPLICABLE LAWS. IN NO EVENT SHALL THE DEVELOPER BE HELD LIABLE FOR SPECIAL COLLATERAL, INCIDENTAL OR CONSEQUENTIAL LIABILITY IN CONNECTION WITH THE USE OF THIS DIGITAL DATA ONCE RELEASED FROM THE DEVELOPER'S OFFICE. THIS DRAWING IS TO BE READ & UNDERSTOOD IN CONJUNCTION WITH THE STRUCTURAL, MECHANICAL, ELECTRICAL & / OR ANY OTHER CONSULTANT'S DOCUMENTATION AS MAY BE APPLICABLE TO THE PROJECT PRIOR TO THE START OF ANY WORKS AND FOR ITS DURATION.

RUBY HOMES


PROJECT:
52 DRINKWATER AVENUE
LOT 42 52 DRINKWATER AVENUE ROUSE HILL

DRAWING TITLE:
ELEVATION 01

NORTH:

LOT NO:	DATE:	SCALE:	DRAWING No:	REV:
42	22-05-2024	1 : 100	CC.08	1
DRAWN BY: AS	CHECKED BY: RH			ISSUED BY:
DRAFTED BY: SL	CLIENT NAME: Owner			


A3

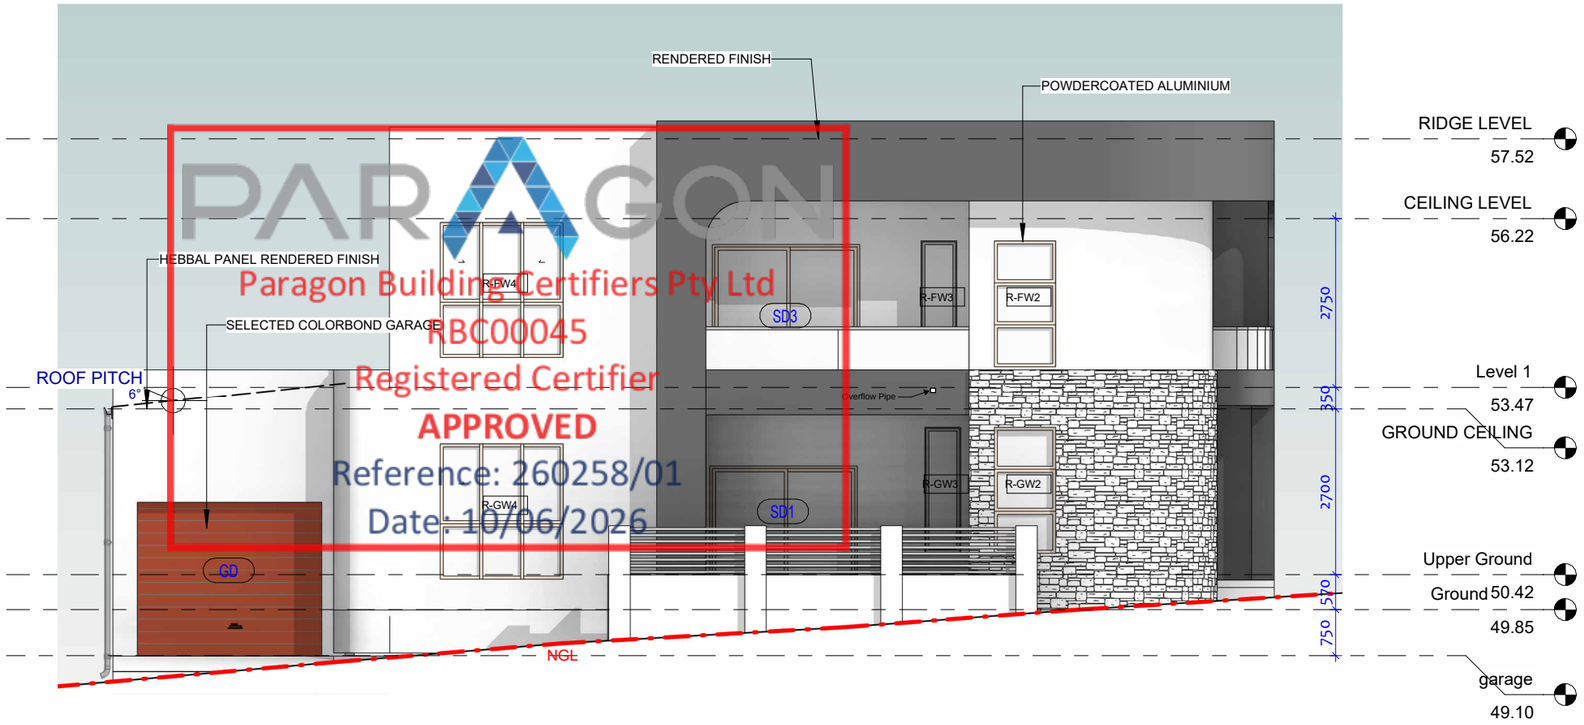

PARAGON
Paragon Building Certifiers Pty Ltd
RBC00045
Registered Certifier
APPROVED
Reference: 260258/01
Date: 10/06/2026

1 SOUTH EAST ELEVATION

1 : 100

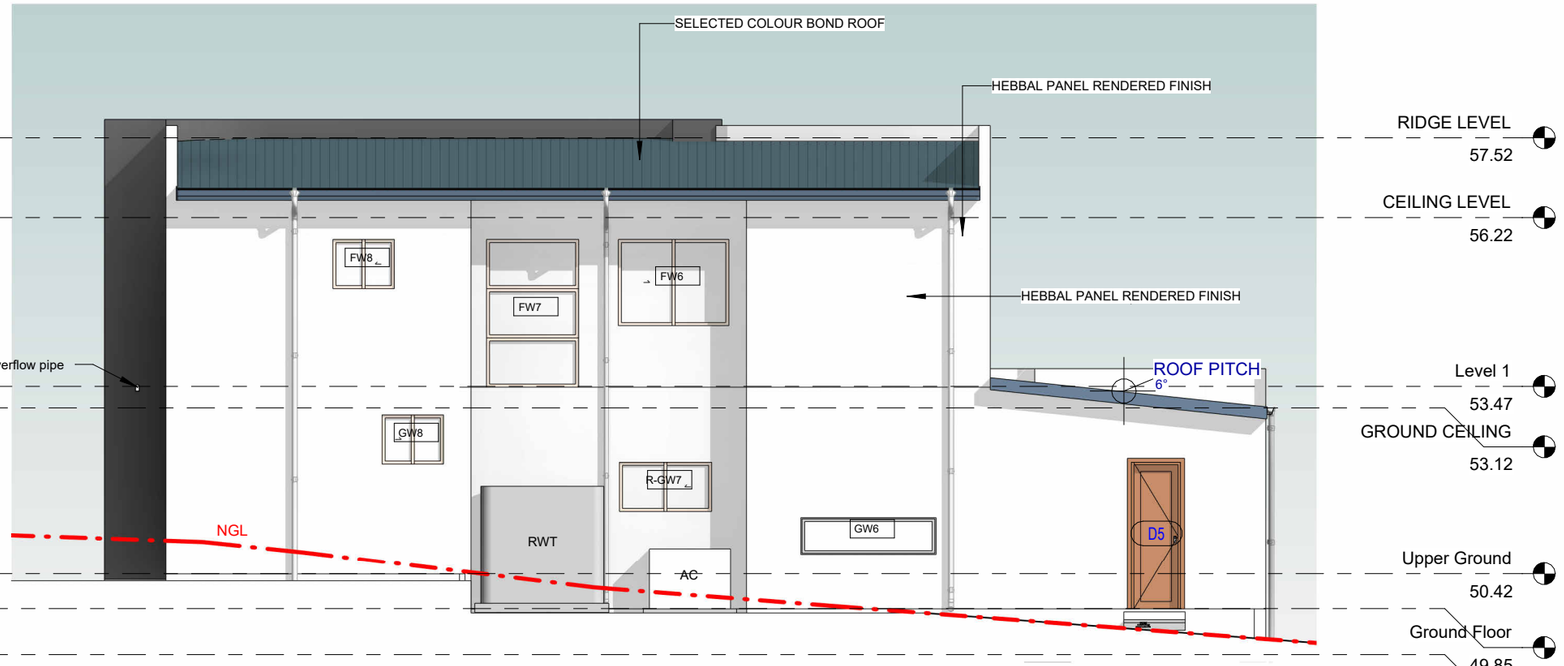

2 NORTH WEST ELEVATION

1 : 100

REV	DATE	DESCRIPTION	BY
1	28-04-2026	Revision 1	

THIS DRAWING IS THE EXCLUSIVE PROPERTY OF THE DEVELOPER & THE REPRODUCTION OF ANY PART WITHOUT THE PRIOR WRITTEN CONSENT OF THE DEVELOPER IS A VIOLATION OF APPLICABLE LAWS. IN NO EVENT SHALL THE DEVELOPER BE HELD LIABLE FOR SPECIAL, COLLATERAL, INCIDENTAL OR CONSEQUENTIAL LIABILITY IN CONNECTION WITH THE USE OF THIS DIGITAL DATA ONCE RELEASED FROM THE DEVELOPER'S OFFICE. THIS DRAWING IS TO BE READ & UNDERSTOOD IN CONJUNCTION WITH THE STRUCTURAL, MECHANICAL, ELECTRICAL & / OR ANY OTHER CONSULTANT'S DOCUMENTATION AS MAY BE APPLICABLE TO THE PROJECT PRIOR TO THE START OF ANY WORKS AND FOR ITS DURATION.

RUBY HOMES

PROJECT:
52 DRINKWATER AVENUE
LOT 42 52 DRINKWATER AVENUE ROUSE HILL


DRAWING TITLE:
ELEVATION 02

NORTH:

CC ISSUE

LOT NO:	DATE:	SCALE:	DRAWING No:	REV:
42	22-05-2024	1 : 100	CC.09	1
DRAWN BY: AS	CHECKED BY: RH			ISSUED BY:
DRAFTED BY: SL	CLIENT NAME: Owner			


A3

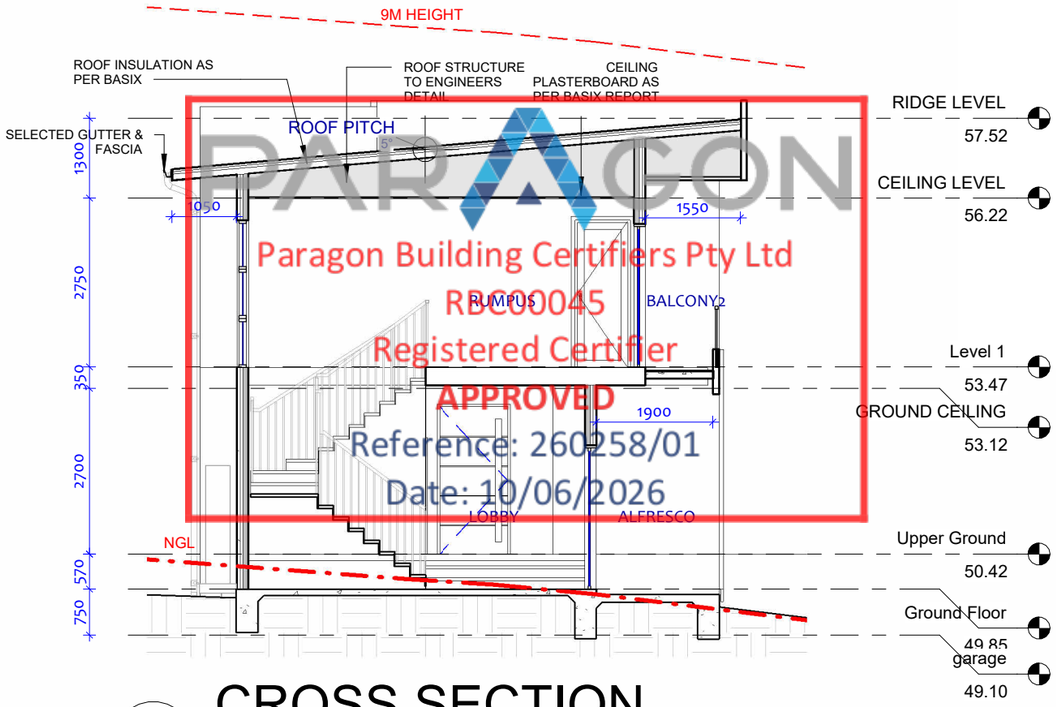

CROSS SECTION

2

1 : 100

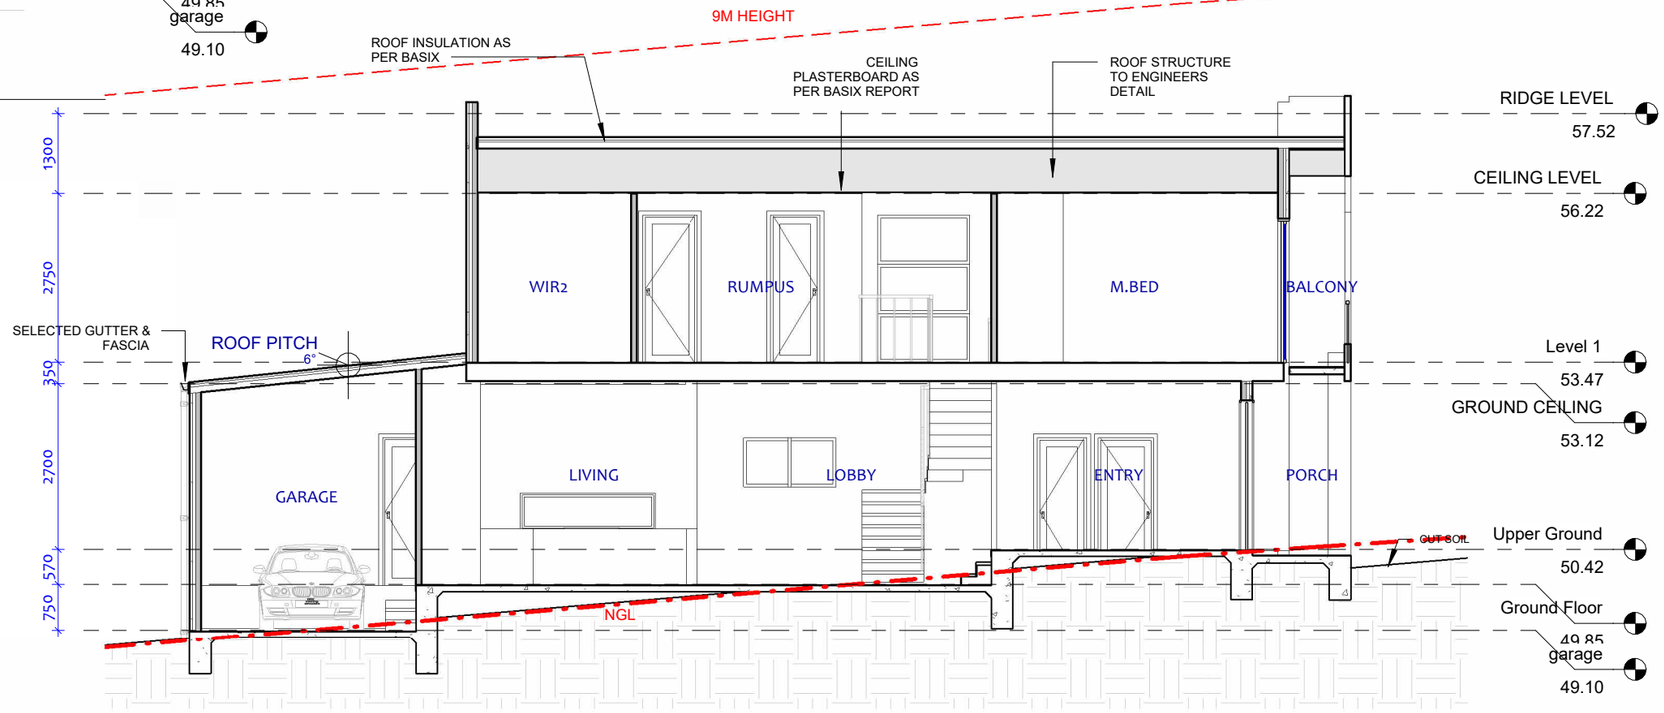

LONGITUDINAL SECTION

1

1 : 100

Paragon Building Certifiers Pty Ltd
RBC000045
Registered Certifier
APPROVED
Reference: 260258/01
Date: 10/06/2026

CC ISSUE

REV	DATE	DESCRIPTION	BY
1	28-04-2026	Revision 1	

THIS DRAWING IS THE EXCLUSIVE PROPERTY OF THE DEVELOPER & THE REPRODUCTION OF ANY PART WITHOUT THE PRIOR WRITTEN CONSENT OF THE DEVELOPER IS A VIOLATION OF APPLICABLE LAWS. IN NO EVENT SHALL THE DEVELOPER BE HELD LIABLE FOR SPECIAL COLLATERAL, INCIDENTAL OR CONSEQUENTIAL LIABILITY IN CONNECTION WITH THE USE OF THIS DIGITAL DATA ONCE RELEASED FROM THE DEVELOPER'S OFFICE. THIS DRAWING IS TO BE READ & UNDERSTOOD IN CONJUNCTION WITH THE STRUCTURAL, MECHANICAL, ELECTRICAL & / OR ANY OTHER CONSULTANT'S DOCUMENTATION AS MAY BE APPLICABLE TO THE PROJECT PRIOR TO THE START OF ANY WORKS AND FOR ITS DURATION.

RUBY HOMES

PROJECT:

52 DRINKWATER AVENUE

LOT 42 52 DRINKWATER AVENUE ROUSE HILL


DRAWING TITLE:

SECTIONS

NORTH:

LOT NO:	DATE:	SCALE:	DRAWING No:	REV:
42	22-05-2024	1 : 100	CC.10	1
DRAWN BY: AS	CHECKED BY: RH			ISSUED BY:
DRAFTED BY: SL	CLIENT NAME: Owner			

A3

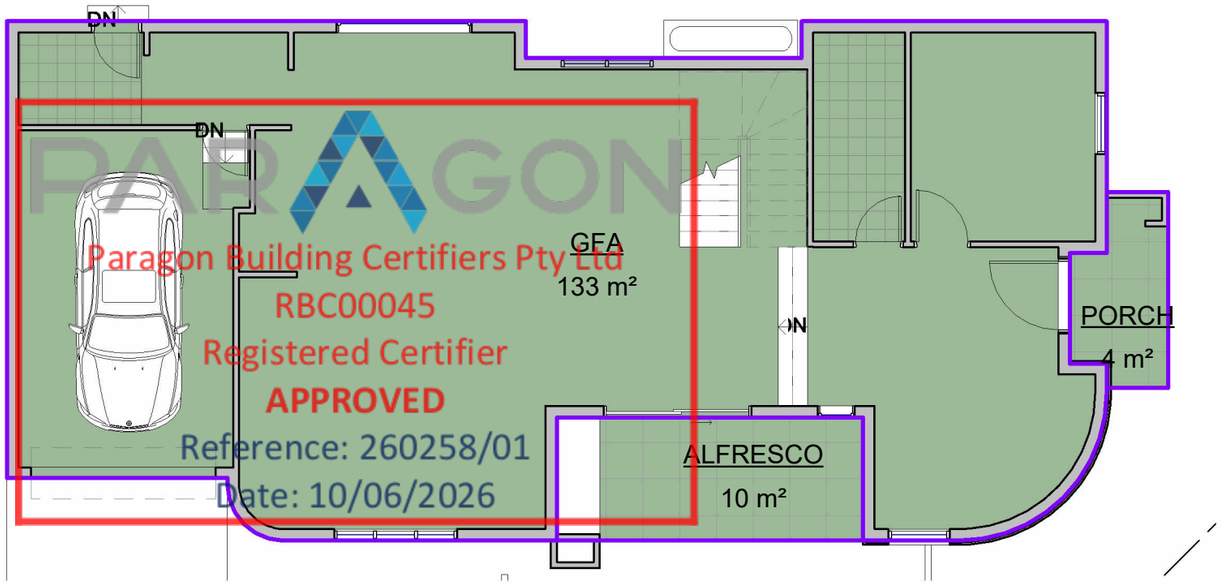


PARAGON
Paragon Building Certifiers Pty Ltd
RBC00045
Registered Certifier
APPROVED
Reference: 260258/01
Date: 10/06/2026

1 Ground Floor

1 : 100

Area Schedule (Gross Building)	
Name	Area
Ground Floor	
GFA	133 m²
PORCH	4 m²
ALFRESCO	10 m²
Ground Floor: 3	147 m²
Level 1	
FFA	105 m²
BALCONY	3 m²
BALCONY2	5 m²
Level 1: 3	113 m²
Grand total: 6	260 m²

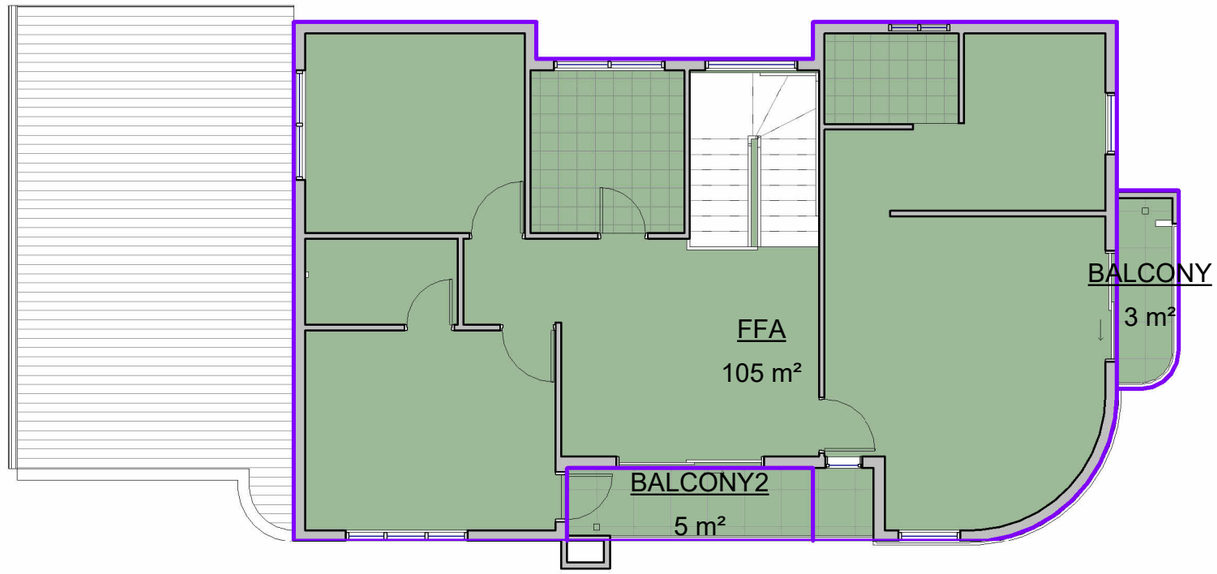

2 Level 1

1 : 100

CC ISSUE

REV	DATE	DESCRIPTION	BY
1	28-04-2026	Revision 1	

THIS DRAWING IS THE EXCLUSIVE PROPERTY OF THE DEVELOPER & THE REPRODUCTION OF ANY PART WITHOUT THE PRIOR WRITTEN CONSENT OF THE DEVELOPER IS A VIOLATION OF APPLICABLE LAWS. IN NO EVENT SHALL THE DEVELOPER BE HELD LIABLE FOR SPECIAL COLLATERAL, INCIDENTAL OR CONSEQUENTIAL LIABILITY IN CONNECTION WITH THE USE OF THIS DIGITAL DATA ONCE RELEASED FROM THE DEVELOPER'S OFFICE. THIS DRAWING IS TO BE READ & UNDERSTOOD IN CONJUNCTION WITH THE STRUCTURAL, MECHANICAL, ELECTRICAL & / OR ANY OTHER CONSULTANT'S DOCUMENTATION AS MAY BE APPLICABLE TO THE PROJECT PRIOR TO THE START OF ANY WORKS AND FOR ITS DURATION.

RUBY HOMES

PROJECT:

52 DRINKWATER AVENUE

LOT 42 52 DRINKWATER AVENUE ROUSE HILL


DRAWING TITLE:

FLOOR AREA PLAN

NORTH:

LOT NO:	DATE:	SCALE:	DRAWING No:	REV:
42	22-05-2024	1 : 100	CC.11	1
DRAWN BY: AS	CHECKED BY: RH			ISSUED BY:
DRAFTED BY: SL	CLIENT NAME: Owner			


A3

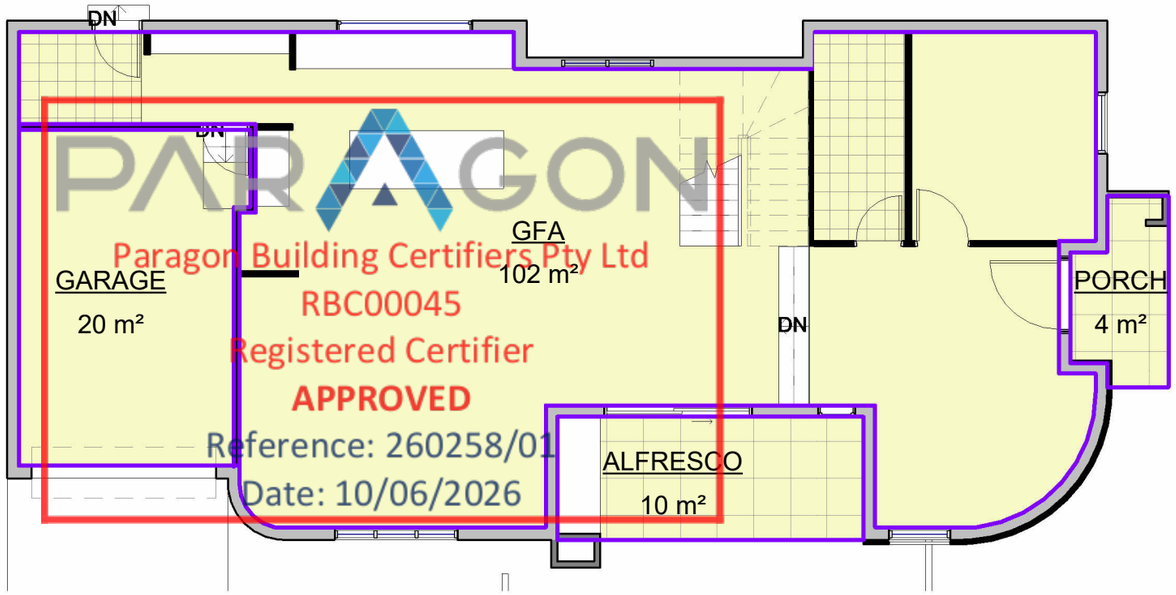

1 Ground Floor

1 : 100

Area Schedule (Rentable)	
Name	Area
Ground Floor	
GARAGE	20 m²
GFA	102 m²
PORCH	4 m²
ALFRESCO	10 m²
Ground Floor: 4	135 m²
Level 1	
FFA	89 m²
VOID	6 m²
BALCONY2	6 m²
BALCONY	3 m²
Level 1: 4	103 m²
Grand total: 8	239 m²

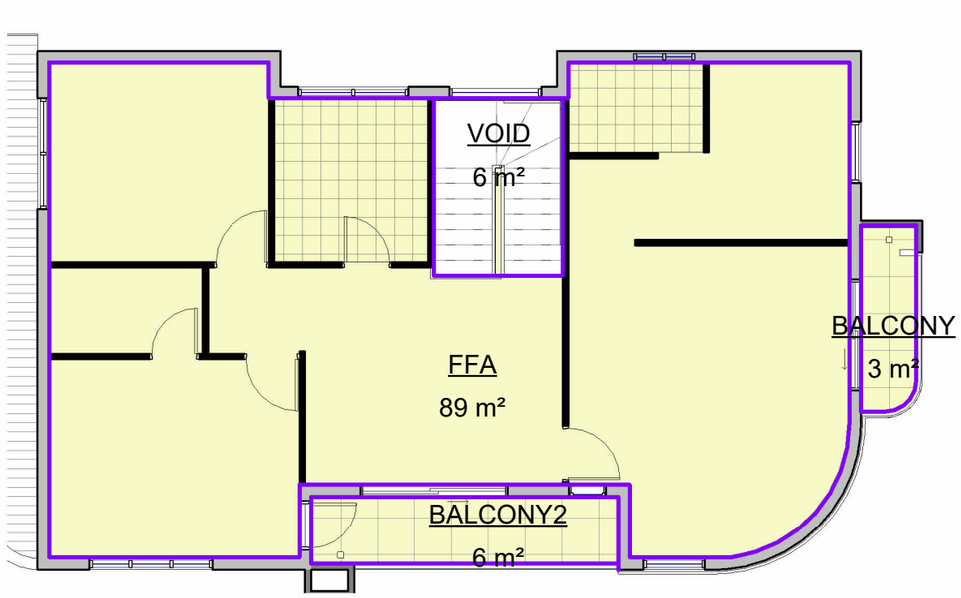

2 Level 1

1 : 100

CC ISSUE

REV	DATE	DESCRIPTION	BY
1	28-04-2026	Revision 1	

THIS DRAWING IS THE EXCLUSIVE PROPERTY OF THE DEVELOPER & THE REPRODUCTION OF ANY PART WITHOUT THE PRIOR WRITTEN CONSENT OF THE DEVELOPER IS A VIOLATION OF APPLICABLE LAWS. IN NO EVENT SHALL THE DEVELOPER BE HELD LIABLE FOR SPECIAL COLLATERAL, INCIDENTAL OR CONSEQUENTIAL LIABILITY IN CONNECTION WITH THE USE OF THIS DIGITAL DATA ONCE RELEASED FROM THE DEVELOPER'S OFFICE. THIS DRAWING IS TO BE READ & UNDERSTOOD IN CONJUNCTION WITH THE STRUCTURAL, MECHANICAL, ELECTRICAL & / OR ANY OTHER CONSULTANT'S DOCUMENTATION AS MAY BE APPLICABLE TO THE PROJECT PRIOR TO THE START OF ANY WORKS AND FOR ITS DURATION.

RUBY HOMES

PROJECT:

52 DRINKWATER AVENUE

LOT 42 52 DRINKWATER AVENUE ROUSE HILL


DRAWING TITLE:

RENTABLE AREA PLAN

NORTH:

LOT NO: 42	DATE: 22-05-2024	SCALE: 1 : 100	DRAWING No: CC.12	REV: 1	
DRAWN BY: AS	CHECKED BY: RH			ISSUED BY:	
DRAFTED BY: SL	CLIENT NAME: Owner				

A3

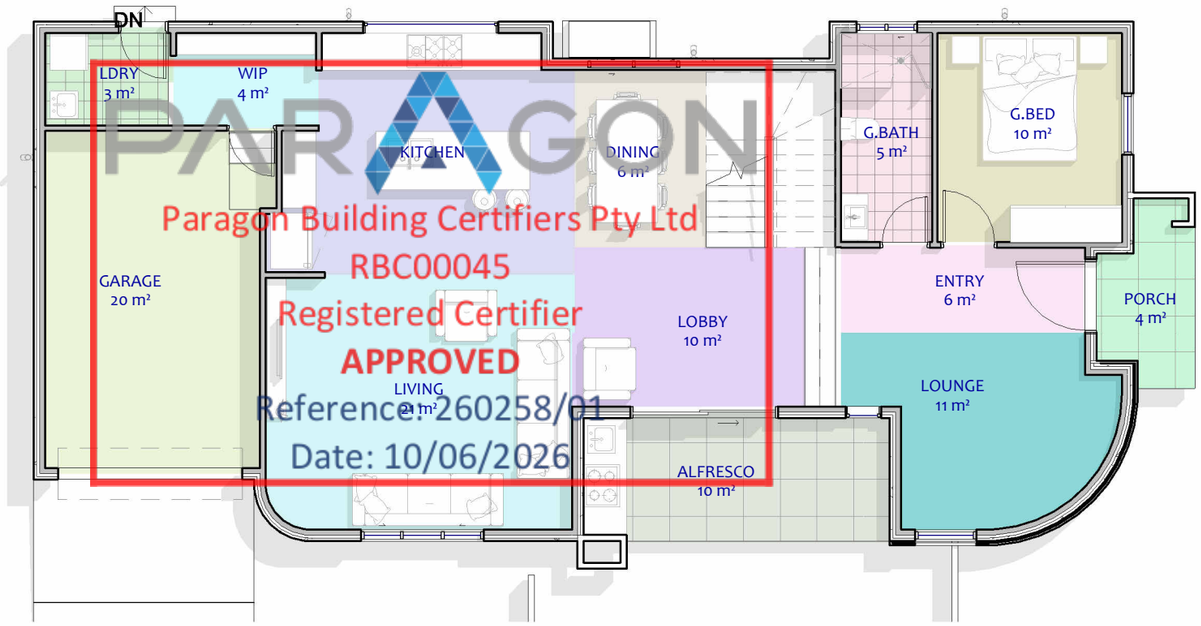


PARAGON
Paragon Building Certifiers Pty Ltd
RBC00045
Registered Certifier
APPROVED
Reference: 260258/01
Date: 10/06/2026

1 Ground Floor Room Area Plan

1 : 100

ALFRESCO
DINING
ENTRY
G.BATH
G.BED
GARAGE
KITCHEN
LDRY
LIVING
LOBBY
LOUNGE
PORCH
WIP

Room Schedule	
Name	Area
Ground Floor	
ALFRESCO	10 m²
DINING	6 m²
ENTRY	6 m²
G.BATH	5 m²
G.BED	10 m²
GARAGE	20 m²
KITCHEN	18 m²
LDRY	3 m²
LIVING	21 m²
LOBBY	10 m²
LOUNGE	11 m²
PORCH	4 m²
WIP	4 m²
Ground Floor: 13	127 m²
Level 1	
BALCONY	3 m²
BALCONY2	5 m²
BATH	7 m²
BED2	13 m²
BED3	12 m²
ENS	3 m²
M.BED	24 m²
RUMPUS	17 m²
STAIRCASE	6 m²
WIR	7 m²
WIR2	4 m²
Level 1: 11	100 m²
Grand total	228 m²

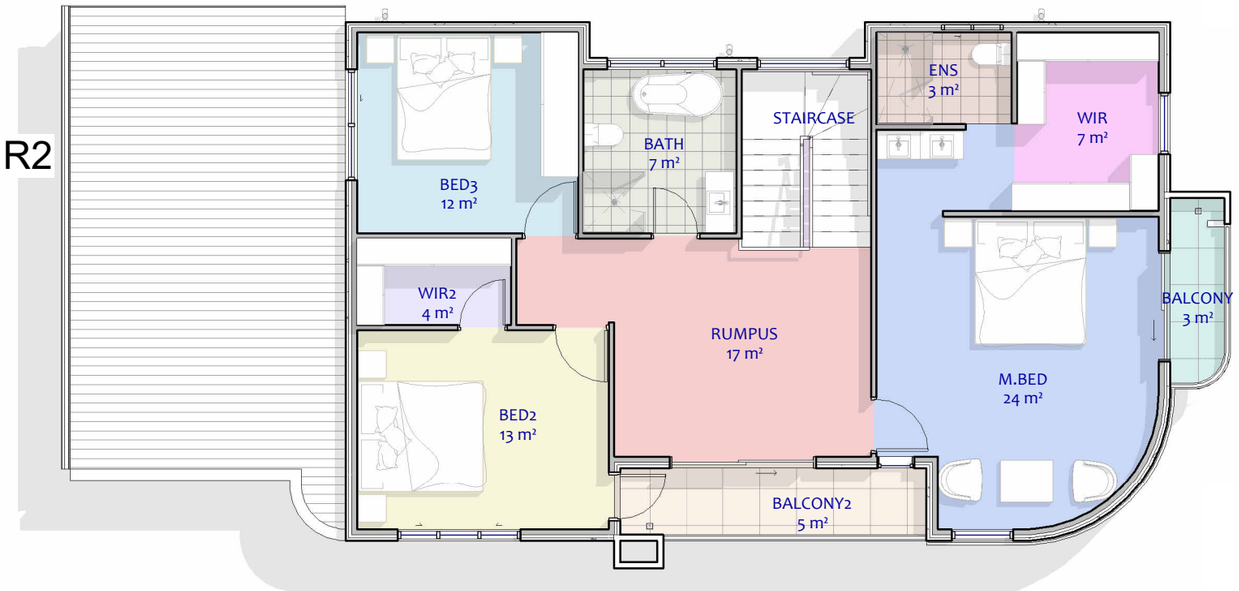

2 Level 1 Room Area Plan

1 : 100

BALCONY
BALCONY2
BATH
BED2
BED3
ENS
M.BED
RUMPUS
STAIRCASE
WIR
WIR2

CC ISSUE

REV	DATE	DESCRIPTION	BY
1	28-04-2026	Revision 1	

THIS DRAWING IS THE EXCLUSIVE PROPERTY OF THE DEVELOPER & THE REPRODUCTION OF ANY PART WITHOUT THE PRIOR WRITTEN CONSENT OF THE DEVELOPER IS A VIOLATION OF APPLICABLE LAWS. IN NO EVENT SHALL THE DEVELOPER BE HELD LIABLE FOR SPECIAL COLLATERAL, INCIDENTAL OR CONSEQUENTIAL LIABILITY IN CONNECTION WITH THE USE OF THIS DIGITAL DATA ONCE RELEASED FROM THE DEVELOPER'S OFFICE. THIS DRAWING IS TO BE READ & UNDERSTOOD IN CONJUNCTION WITH THE STRUCTURAL, MECHANICAL, ELECTRICAL & / OR ANY OTHER CONSULTANT'S DOCUMENTATION AS MAY BE APPLICABLE TO THE PROJECT PRIOR TO THE START OF ANY WORKS AND FOR ITS DURATION.

RUBY HOMES

PROJECT:
52 DRINKWATER AVENUE
LOT 42 52 DRINKWATER AVENUE ROUSE HILL

DRAWING TITLE:
ROOM AREA PLAN

NORTH:

LOT NO:	DATE:	SCALE:	DRAWING No:	REV:
42	22-05-2024	1 : 100	CC.13	1
DRAWN BY: AS	CHECKED BY: RH			ISSUED BY:
DRAFTED BY: SL	CLIENT NAME: Owner			

A3




PARAGON
Paragon Building Certifiers Pty Ltd
RBC00045
Registered Certifier
APPROVED
Reference: 260258/01
Date: 10/06/2026

1 FRONT FACADE-DRINKWATER AVENUE VIEW



2 SPROWLE STREET VIEW

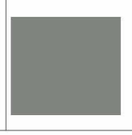	1. RF	2. HEB	3. CD1	4. CR1	5. AL	6. ED	7. GD	8. FAS	9. GUT
	ROOF	MAIN WALLS	CLADDING	ACCENT 1/RENDER	WINDOWS/ BALUSTRADE	MAIN DOOR	GARAGE DOOR	FASCIA	GUTTER
MATERIAL	COLORBOND DARK MONUMENT	HEBEL	BLUEBOARD	HEBEL	ALUMINIUM	TIMBER	COLORBOND	COLORBOND	COLORBOND
COLOUR									

NOTE : ALL COLOURS SPECIFIED ARE INDICATATIVE ONLY AND ARE SUBJECT TO VARIATION AND TO AVAILABILITY
ANY DISCREPANCY PLEASE FOLLOW AS PER RENDERED IMAGE

CC ISSUE

REV	DATE	DESCRIPTION	BY
1	28-04-2026	Revision 1	

THIS DRAWING IS THE EXCLUSIVE PROPERTY OF THE DEVELOPER & THE REPRODUCTION OF ANY PART WITHOUT THE PRIOR WRITTEN CONSENT OF THE DEVELOPER IS A VIOLATION OF APPLICABLE LAWS. IN NO EVENT SHALL THE DEVELOPER BE HELD LIABLE FOR SPECIAL COLLATERAL, INCIDENTAL OR CONSEQUENTIAL LIABILITY IN CONNECTION WITH THE USE OF THIS DIGITAL DATA ONCE RELEASED FROM THE DEVELOPER'S OFFICE. THIS DRAWING IS TO BE READ & UNDERSTOOD IN CONJUNCTION WITH THE STRUCTURAL, MECHANICAL, ELECTRICAL & / OR ANY OTHER CONSULTANT'S DOCUMENTATION AS MAY BE APPLICABLE TO THE PROJECT PRIOR TO THE START OF ANY WORKS AND FOR ITS DURATION.

RUBY HOMES


PROJECT:
52 DRINKWATER AVENUE
LOT 42 52 DRINKWATER AVENUE ROUSE HILL

DRAWING TITLE:
COLOR SCHEDULE

NORTH:

LOT NO: 42	DATE: 22-05-2024	SCALE: 1 : 100	DRAWING No: CC.14	REV: 1	
DRAWN BY: AS	CHECKED BY: RH			ISSUED BY:	
DRAFTED BY: SL	CLIENT NAME: Owner				

A3

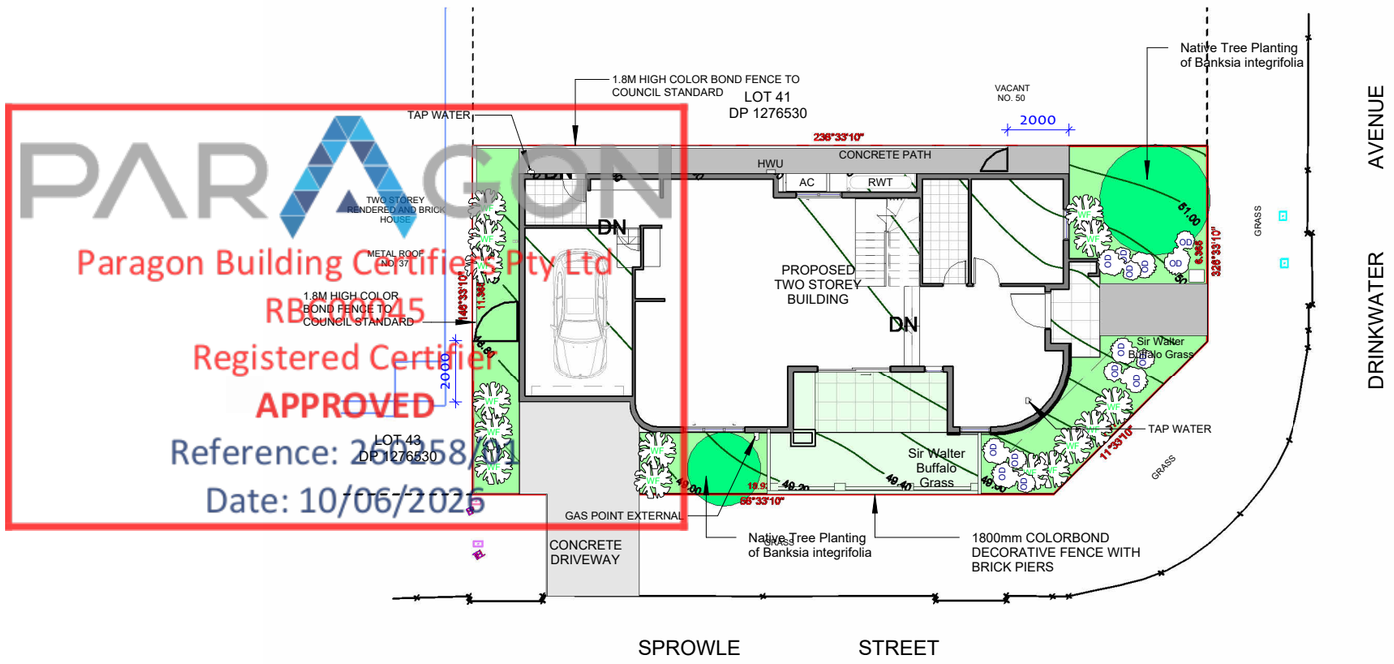


PARAGON
Paragon Building Certifiers Pty Ltd
RBC 445
Registered Certifier
APPROVED
Reference: 250358/01
Date: 10/06/2025

1 CC - LANDSCAPE PLAN

1 : 200

LEGENDS

- PROPOSED TREE PLANTING
- PROPOSED SCREENING PLANTING
- PROPOSED SHRUB PLANTING
- PROPOSED ACCENT PLANTING
- PROPOSED TURF AREA TO BE SIR WALTER SOFT LEAF BUFFALO
- PROPOSED GROUNDCOVER & GRASS PLANTING
- PROPOSED CONCRETE PATH

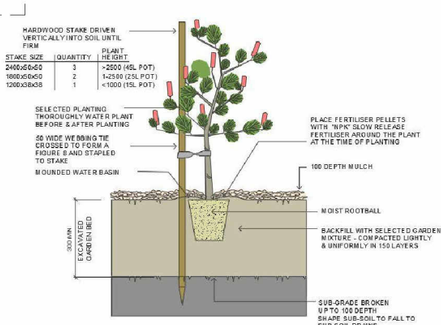

2. TREE & SHRUB PLANTING IN GARDEN BED

NOTE:
DO NOT PLANT IN UNSUITABLE WEATHER CONDITIONS SUCH AS EXTREME HEAT, COLD, WIND OR RAIN
CLAY SOIL IS TO BE TREATED WITH CLAY BREAKER AND ORGANIC COMPOST

GENERAL NOTES:

- LANDSCAPE CONTRACTOR TO CHECK DA CONDITIONS AND STAMPED LANDSCAPE PLAN
- BEFORE COMMENCING WORKS TO ENSURE NO ADDITIONS/AMENDMENTS TO PLAN.
- GARDEN BEDS IN OSD BASIN TO CONSIST OF NON FLOATABLE DECORATIVE GRAVEL.
- REFER TO HYDRAULICS ENGINEERS PLAN FOR OSD DETAILS/FINAL LEVELS.
- MULCHED PLANTING BEDS TO BE A MINIMUM DEPTH OF 75mm AS SELECTED.
- CONTRACTOR'S RESPONSIBILITY TO CHECK AND ADJUST SOIL pH AS REQUIRED.
- PROVIDE TIMBER EDGE AS A MINIMUM BENEATH FENCING/GATES TO DEFINE TURF AND GARDEN BEDS/PATHWAYS,EDGING TO BE PROVIDED TO ALL AREAS WHERE DIFFERING MATERIALS MEET i.e TURF/GARDEN,TURF/GRAVEL PATH ETC.
- WEED MAT BENEATH GRAVEL GRAVEL PATHWAYS REQUIRED TO LIMIT MUD TRACKING.
- PREMIUM ORGANIC GARDEN MIX TO BE USED.
- ALL PLANTS TO BE HEALTHY AND VIGOROUS.
- CONTRACTOR TO MAKE GOOD TURF ON NATURE STRIP POST CONSTRUCTION
- CONTRACTOR TO MAKE GOOD TURF ON NATURE STRIP POST CONSTRUCTION.
- DO NOT SCALE ARCHITECTURAL SETOUT FROM LANDSCAPE DRAWING.
- EXISTING TREE SPREAD APPROXIMATE ONLY.REFER TO TREE REPORT WHEN APPLICABLE.
- SITE SURVEY PROVIDED BY OTHERS.
- BUFFALO TURF PREFERRED OVER KIKUYU.


LANDSCAPE BASIX NOTE:
THE APPLICANT MUST PLANT INDIGENEOUS OR LOW WATER USE SPECIES OF VEGETATION THROUGHOUT 15 SQM OF THE SITE.

NOTE :BUILDER RESERVES THE RIGHT NOT TO UNDERTAKE NOR SUPPLY CERTIFICATE FOR OCCUPATION CERTIFICATE.
NOTE : TO AID COMPLIANCE WITH BASIX LEGISLATION,PLANTS (WHERE APPLICABLE) HAVE BEEN SELECTED FROM THE LOCAL CITY COUNCIL/SHIRE PLANT LISTS.
NOTE: LOCATION OF SEWER MAINS/LINES,WATER PIPES,UNDERGROUND ELECTRICITY AND OTHER SERVICES MUST BE OBTAINED PRIOR TO COMMENCEMENT OF ANY WORK ON SITE.

CONTRACTORS NOTE : CALCULATED ARES DETERMINED BY CAD AND HAVE BEEN ROUNDED UP FOR USE AS A GUIDE ONLY ALLOW STANDARD PERCENTAGE FOR CUTTING AND WASTAGE .CONFIRM DIMENSIONS AND NUMBERS PRIOR TO QUOTING/ORDERING.

PLANT SCHEDULE

Genus	Common Name	Qty	Pot size	Height	width
Trees					
Banksia integrifolia	coast banksia	2	45L	7	4
Cupaniopsis anacardioides	Tuckeroo	1	45L	8	4
Shrubs					
Grevillea 'moonlight'	Grevillea Moonlight	-	140mm	3	1.5
Leptospermum 'Cardwell'	Tea Tree	-	140mm	1.5	1
Leucophyta Brownii	Cushion Bush	-	140mm	1.5	1
Westringia Fruticosa	Coastal Rosemary	-	140mm	1.5	2
Accents					
Agave Americana	American Aloe	-	200mm	1.5	1.5

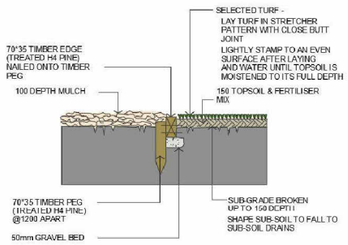

1. TURF & GARDEN EDGE DETAIL

NOTE:
ALIGNMENT OF BRICK EDGE SHALL BE EVEN & FREE FROM DIPS AND HUMPS.

CC ISSUE

REV	DATE	DESCRIPTION	BY
1	28-04-2026	Revision 1	

THIS DRAWING IS THE EXCLUSIVE PROPERTY OF THE DEVELOPER & THE REPRODUCTION OF ANY PART WITHOUT THE PRIOR WRITTEN CONSENT OF THE DEVELOPER IS A VIOLATION OF APPLICABLE LAWS. IN NO EVENT SHALL THE DEVELOPER BE HELD LIABLE FOR SPECIAL COLLATERAL, INCIDENTAL OR CONSEQUENTIAL LIABILITY IN CONNECTION WITH THE USE OF THIS DIGITAL DATA ONCE RELEASED FROM THE DEVELOPER'S OFFICE. THIS DRAWING IS TO BE READ & UNDERSTOOD IN CONJUNCTION WITH THE STRUCTURAL, MECHANICAL, ELECTRICAL & / OR ANY OTHER CONSULTANT'S DOCUMENTATION AS MAY BE APPLICABLE TO THE PROJECT PRIOR TO THE START OF ANY WORKS AND FOR ITS DURATION.

RUBY HOMES

PROJECT:
52 DRINKWATER AVENUE
LOT 42 52 DRINKWATER AVENUE ROUSE HILL

DRAWING TITLE:
LANDSCAPE PLAN

NORTH:

LOT NO:	DATE:	SCALE:	DRAWING No:	REV:
42	22-05-2024	1 : 200	CC.15	1
DRAWN BY: AS	CHECKED BY: RH			ISSUED BY:
DRAFTED BY: SL	CLIENT NAME: Owner			

A3

BASIX™ Certificate

Building Sustainability Index
www.planningportal.nsw.gov.au/development-and-assessment/basix

Single Dwelling

Certificate number: 1741551S_04

This certificate confirms that the proposed development will meet the NSW government's requirements for sustainability, if it is built in accordance with the commitments set out below. Terms used in this certificate, or in the commitments, have the meaning given by the document entitled "BASIX Definitions" dated 10/09/2020 published by the Department. This document is available at www.planningportal.nsw.gov.au/definitions

This certificate is a revision of certificate number 1741551S lodged with the consent authority or certifier on 30 May 2024 with application PAN-430811.

It is the responsibility of the applicant to verify with the consent authority that the original, or any revised certificate, complies with the requirements of Schedule 1 Clause 2A, 4A or 6A of the Environment Planning and Assessment Regulation 2000.

Secretary
Date of issue: Friday, 13 June 2025
To be valid, this certificate must be lodged within 3 months of the date of issue.

Project summary	
Project name	Lot 42 52 Drinkwater Avenue Rouse Hill_04
Street address	52 DRINKWATER Avenue ROUSE HILL 2155
Local Government Area	Blacktown City Council
Plan type and plan number	Deposited Plan DP1276530
Lot no.	42
Section no.	-
Project type	separate dwelling house
No. of bedrooms	4

Project score		
Water	✔ 46	Target 40
Thermal Performance	✔ Pass	Target Pass
Energy	✔ 54	Target 50
Materials	✔ -1	Target n/a

Certificate Prepared by
Name / Company Name: Ruby Homes
ABN (if applicable):

PARAGON
Paragon Building Certifiers Pty Ltd
RBC00045
Registered Certifier
APPROVED
Reference: 260258/01
Date: 10/06/2026

Description of project

Project address	
Project name	Lot 42 52 Drinkwater Avenue Rouse Hill_04
Street address	52 DRINKWATER Avenue ROUSE HILL 2155
Local Government Area	Blacktown City Council
Plan type and plan number	Deposited Plan DP1276530
Lot no.	42
Section no.	-
Project type	
Project type	separate dwelling house
No. of bedrooms	4
Site details	
Site area (m²)	259
Roof area (m²)	159
Conditioned floor area (m²)	150.0
Unconditioned floor area (m²)	15.0
Total area of garden and lawn (m²)	81
Roof area of the existing dwelling (m²)	0

Assessor details and thermal loads	
NatHERS assessor number	n/a
NatHERS certificate number	n/a
Climate zone	n/a
Area adjusted cooling load (MJ/m².year)	n/a
Area adjusted heating load (MJ/m².year)	n/a
Ceiling fan in at least one bedroom	n/a
Ceiling fan in at least one living room or other conditioned area	n/a

Project score		
Water	✔ 46	Target 40
Thermal Performance	✔ Pass	Target Pass
Energy	✔ 54	Target 50
Materials	✔ -1	Target n/a

Schedule of BASIX commitments

The commitments set out below regulate how the proposed development is to be carried out. It is a condition of any development consent granted, or complying development certificate issued, for the proposed development, that BASIX commitments be complied with.

Water Commitments	Show on DA plans	Show on CC/CDC plans & specs	Certifier check
Fixtures			
The applicant must install showerheads with a minimum rating of 4 star (> 4.5 but <= 6 L/min plus spray force and/or coverage tests) in all showers in the development.		✔	✔
The applicant must install a toilet flushing system with a minimum rating of 4 star in each toilet in the development.		✔	✔
The applicant must install taps with a minimum rating of 4 star in the kitchen in the development.		✔	
The applicant must install basin taps with a minimum rating of 4 star in each bathroom in the development.		✔	
Alternative water			
Rainwater tank			
The applicant must install a rainwater tank of at least 2000 litres on the site. This rainwater tank must meet, and be installed in accordance with, the requirements of all applicable regulatory authorities.	✔	✔	✔
The applicant must configure the rainwater tank to collect rain runoff from at least 159 square metres of the roof area of the development (excluding the area of the roof which drains to any stormwater tank or private dam).		✔	✔
The applicant must connect the rainwater tank to: • the cold water tap that supplies each clothes washer in the development		✔	✔
• at least one outdoor tap in the development (Note: NSW Health does not recommend that rainwater be used for human consumption in areas with potable water supply.)		✔	✔

Thermal Comfort Commitments	Show on DA plans	Show on CC/CDC plans & specs	Certifier check
Do-it-yourself Method			
General features			
The dwelling must not have more than 2 storeys.	✔	✔	✔
The conditioned floor area of the dwelling must not exceed 300 square metres.	✔	✔	✔
The dwelling must not contain open mezzanine area exceeding 25 square metres.	✔	✔	✔
The dwelling must not contain third level habitable attic room.	✔	✔	✔
Floor, walls and ceiling/roof			
The applicant must construct the floor(s), walls, and ceiling/roof of the dwelling in accordance with the specifications listed in the table below.	✔	✔	✔

Construction	Additional insulation required (R-Value)	Other specifications
floor - concrete slab on ground	nil	
external wall - AAC veneer (AAC: 75 mm)	2.79 (or 3.60 including construction)	
internal wall shared with garage - plasterboard	nil	
ceiling and roof - flat ceiling / flat roof, framed	ceiling: 5 (up), roof: foil backed blanket (75 mm)	framed; medium (solar absorptance 0.475-0.70)

Note	• Insulation specified in this Certificate must be installed in accordance with Part 3.12.1.1 of the Building Code of Australia.
Note	• In some climate zones, insulation should be installed with due consideration of condensation and associated interaction with adjoining building materials.

Thermal Comfort Commitments	Show on DA plans	Show on CC/CDC plans & specs	Certifier check
Windows, glazed doors and skylights			
The applicant must install the windows, glazed doors and shading devices described in the table below, in accordance with the specifications listed in the table. Relevant overshadowing specifications must be satisfied for each window and glazed door.	✔	✔	✔
The dwelling may have 1 skylight (<0.7 square metres) which is not listed in the table.	✔	✔	✔
The following requirements must also be satisfied in relation to each window and glazed door: • For the following glass and frame types, the certifier check can be performed by visual inspection. - Aluminium single clear - Aluminium double (air) clear - Timber/uPVC/fibreglass single clear - Timber/uPVC/fibreglass double (air) clear	✔	✔	✔ ✔
• Overshadowing buildings/vegetation must be of the height and distance from the centre and the base of the window and glazed door, as specified in the 'overshadowing' column.	✔	✔	✔

Window/glazed door no.	Maximum height (mm)	Maximum width (mm)	Type	Shading Device (Dimension within 10%)	Overshadowing
North-East facing					
GW1	2050.00	1000.00	aluminium, single, clear	eave 600 mm, 3400 mm above head of window or glazed door	>4 m high, 8-12 m away
FW1	1800.00	1000.00	aluminium, single, clear	eave 600 mm, 350 mm above head of window or glazed door	>4 m high, 8-12 m away
SD2	2300.00	1800.00	aluminium, single, clear	eave 1000 mm, 710 mm above head of window or glazed door	>4 m high, 8-12 m away

Window/glazed door no.	Maximum height (mm)	Maximum width (mm)	Type	Shading Device (Dimension within 10%)	Overshadowing
MD	2400.00	1120.00	timber/UPVC/fibreglass, single, clear	solid overhang 1600 mm, 310 mm above head of window or glazed door	>4 m high, 8-12 m away
South-East facing					
SD1	2300.00	2400.00	aluminium, single, clear	solid overhang 2000 mm, 980 mm above head of window or glazed door	>4 m high, 8-12 m away
SD3	2300.00	2400.00	aluminium, single, clear	eave 1310 mm, 410 mm above head of window or glazed door	>4 m high, 8-12 m away
R-GW2	2050.00	1000.00	aluminium, single, clear	eave 450 mm, 3700 mm above head of window or glazed door	>4 m high, 8-12 m away
R-GW3	2050.00	600.00	aluminium, single, clear	solid overhang 1200 mm, 200 mm above head of window or glazed door	>4 m high, 8-12 m away
R-GW4	2200.00	2000.00	aluminium, single, clear	none	>4 m high, 8-12 m away
R-FW2	2050.00	1000.00	aluminium, single, clear	eave 450 mm, 650 mm above head of window or glazed door	>4 m high, 8-12 m away
R-FW3	2050.00	600.00	aluminium, single, clear	eave 1650 mm, 650 mm above head of window or glazed door	>4 m high, 8-12 m away
R-FW4	2200.00	2000.00	aluminium, single, clear	none	>4 m high, 8-12 m away
South-West facing					
FW5	1500.00	1800.00	aluminium, single, clear	none	>4 m high, 2-5 m away
North-West facing					
GW6	600.00	2200.00	aluminium, single, clear	eave 250 mm, 5156 mm above head of window or glazed door	>4 m high, 2-5 m away

Window/glazed door no.	Maximum height (mm)	Maximum width (mm)	Type	Shading Device (Dimension within 10%)	Overshadowing
R-GW7	800.00	1500.00	aluminium, single, clear	eave 850 mm, 3956 mm above head of window or glazed door	>4 m high, 2-5 m away
GW8	800.00	1000.00	aluminium, single, clear	eave 250 mm, 3486 mm above head of window or glazed door	>4 m high, 2-5 m away
FW6	1400.00	1800.00	aluminium, single, clear	eave 850 mm, 636 mm above head of window or glazed door	>4 m high, 2-5 m away
FW7	2400.00	1500.00	aluminium, single, clear	eave 850 mm, 636 mm above head of window or glazed door	>4 m high, 2-5 m away
FW8	800.00	1000.00	aluminium, single, clear	eave 250 mm, 636 mm above head of window or glazed door	>4 m high, 2-5 m away
D5	2340.00	720.00	timber/UPVC/fibreglass, single, clear	eave 250 mm, 830 mm above head of window or	>4 m high, 2-5 m away

Energy Commitments	Show on DA plans	Show on CC/CDC plans & specs	Certifier check
Hot water			
The applicant must install the following hot water system in the development, or a system with a higher energy rating: gas instantaneous with a performance of 5 stars.	✔	✔	✔
Cooling system			
The applicant must install the following cooling system, or a system with a higher energy rating, in at least 1 living area: 3-phase airconditioning; Energy rating: EER 3.0 - 3.5		✔	✔
The applicant must install the following cooling system, or a system with a higher energy rating, in at least 1 bedroom: 3-phase airconditioning; Energy rating: EER 3.0 - 3.5		✔	✔
The cooling system must provide for day/night zoning between living areas and bedrooms.		✔	✔
Heating system			
The applicant must install the following heating system, or a system with a higher energy rating, in at least 1 living area: 3-phase airconditioning; Energy rating: EER 3.0 - 3.5		✔	✔
The applicant must install the following heating system, or a system with a higher energy rating, in at least 1 bedroom: 3-phase airconditioning; Energy rating: EER 3.0 - 3.5		✔	✔
The heating system must provide for day/night zoning between living areas and bedrooms.		✔	✔
Ventilation			
The applicant must install the following exhaust systems in the development: At least 1 Bathroom: no mechanical ventilation (ie. natural); Operation control: n/a		✔	✔
Kitchen: individual fan, ducted to façade or roof; Operation control: manual switch on/off		✔	✔
Laundry: natural ventilation only, or no laundry; Operation control: n/a		✔	✔
Artificial lighting			

Energy Commitments	Show on DA plans	Show on CC/CDC plans & specs	Certifier check
The applicant must ensure that the "primary type of artificial lighting" is fluorescent or light emitting diode (LED) lighting in each of the following rooms, and where the word "dedicated" appears, the fittings for those lights must only be capable of accepting fluorescent or light emitting diode (LED) lamps:			
• at least 4 of the bedrooms / study; dedicated		✔	✔
• at least 4 of the living / dining rooms; dedicated		✔	✔
• the kitchen; dedicated		✔	✔
• all bathrooms/toilets; dedicated		✔	✔
• the laundry; dedicated		✔	✔
• all hallways; dedicated		✔	✔
Natural lighting			
The applicant must install a window and/or skylight in 3 bathroom(s)/toilet(s) in the development for natural lighting.	✔	✔	✔
Other			
The applicant must install a gas cooktop & electric oven in the kitchen of the dwelling.		✔	
The applicant must construct each refrigerator space in the development so that it is "wet ventilated", as defined in the BASIX definitions.		✔	
The applicant must install a fixed outdoor clothes drying line as part of the development.		✔	

Legend
In these commitments, "applicant" means the person carrying out the development.
Commitments identified with a ✔ in the "Show on DA plans" column must be shown on the plans accompanying the development application for the proposed development (if a development application is to be lodged for the proposed development).
Commitments identified with a ✔ in the "Show on CC/CDC plans and specs" column must be shown in the plans and specifications accompanying the application for a construction certificate / complying development certificate for the proposed development.
Commitments identified with a ✔ in the "Certifier check" column must be certified by a certifying authority as having been fulfilled, before a final occupation certificate (either interim or final) for the development may be issued.

REV	DATE	DESCRIPTION	BY
1	28-04-2026	Revision 1	

THIS DRAWING IS THE EXCLUSIVE PROPERTY OF THE DEVELOPER & THE REPRODUCTION OF ANY PART WITHOUT THE PRIOR WRITTEN CONSENT OF THE DEVELOPER IS A VIOLATION OF APPLICABLE LAWS. IN NO EVENT SHALL THE DEVELOPER BE HELD LIABLE FOR SPECIAL COLLATERAL, INCIDENTAL OR CONSEQUENTIAL LIABILITY IN CONNECTION WITH THE USE OF THIS DIGITAL DATA ONCE RELEASED FROM THE DEVELOPER'S OFFICE. THIS DRAWING IS TO BE READ & UNDERSTOOD IN CONJUNCTION WITH THE STRUCTURAL, MECHANICAL, ELECTRICAL & / OR ANY OTHER CONSULTANT'S DOCUMENTATION AS MAY BE APPLICABLE TO THE PROJECT PRIOR TO THE START OF ANY WORKS AND FOR ITS DURATION.

RUBY HOMES

PROJECT:
52 DRINKWATER AVENUE
LOT 42 52 DRINKWATER AVENUE ROUSE HILL

DRAWING TITLE:
BASIX


NORTH:

LOT NO:	DATE:	SCALE:	DRAWING No:	REV:
42	22-05-2024		CC.16	1
DRAWN BY: AS	CHECKED BY: RH			ISSUED BY:
DRAFTED BY: SL	CLIENT NAME: Owner			

CC ISSUE


A3

PARAGON
Paragon Building Certifiers Pty Ltd
RBC00045
Registered Certifier
APPROVED
Reference: 260258/01
Date: 10/06/2026

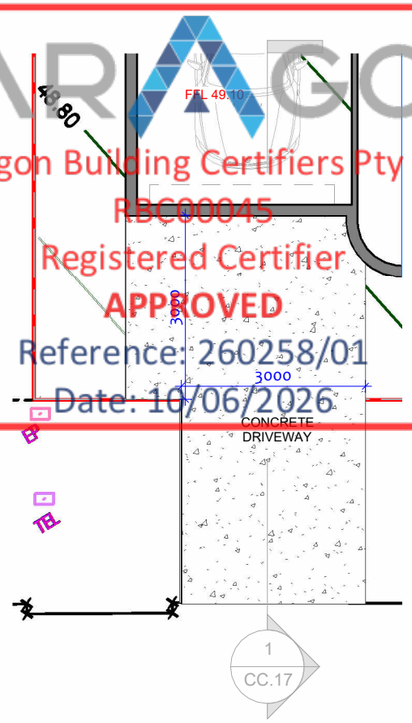

2 DA - DRIVEWAY PLAN

1 : 100

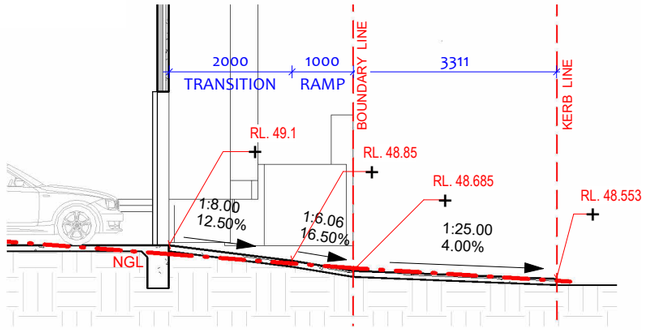

1 DRIVEWAY SECTION

1 : 100

CC ISSUE

REV	DATE	DESCRIPTION	BY
1	28-04-2026	Revision 1	

THIS DRAWING IS THE EXCLUSIVE PROPERTY OF THE DEVELOPER & THE REPRODUCTION OF ANY PART WITHOUT THE PRIOR WRITTEN CONSENT OF THE DEVELOPER IS A VIOLATION OF APPLICABLE LAWS. IN NO EVENT SHALL THE DEVELOPER BE HELD LIABLE FOR SPECIAL COLLATERAL, INCIDENTAL OR CONSEQUENTIAL LIABILITY IN CONNECTION WITH THE USE OF THIS DIGITAL DATA ONCE RELEASED FROM THE DEVELOPER'S OFFICE. THIS DRAWING IS TO BE READ & UNDERSTOOD IN CONJUNCTION WITH THE STRUCTURAL, MECHANICAL, ELECTRICAL & / OR ANY OTHER CONSULTANT'S DOCUMENTATION AS MAY BE APPLICABLE TO THE PROJECT PRIOR TO THE START OF ANY WORKS AND FOR ITS DURATION.

RUBY HOMES

PROJECT:
52 DRINKWATER AVENUE
LOT 42 52 DRINKWATER AVENUE ROUSE HILL

DRAWING TITLE:
DRIVEWAY PLAN

NORTH:

LOT NO: 42	DATE: 22-05-2024	SCALE: 1 : 100	DRAWING No: CC.17	REV: 1	
DRAWN BY: AS	CHECKED BY: RH			ISSUED BY:	
DRAFTED BY: SL	CLIENT NAME: Owner				

A3

ABCB HOUSING PROVISIONS : PART 10.2 WET AREA WATERPROOFING

10.2.1 Wet Areas


1. Building elements in wet areas within a building must be protected with a waterproofing system.
2. The waterproofing system in (1) must be either waterproof or water resistant in accordance with 10.2.2 to 10.2.6.

10.2.2 Shower Area (enclosed and unenclosed)


1. For a shower area with a hob, step-down or level threshold, the following applies:
   a. The floor of the *shower area* must be *waterproof*, including any hob or step-down (see Figure 10.2.2); and
   b. The walls of the *shower area* must be *waterproof* not less than 1800 mm above the floor substrate (see Figure 10.2.2).
   c. Wall junctions and joints within the *shower area* must be *waterproof* not less than 40 mm either side of the junction (see Figure 10.2.2).
   d. Wall/floor junctions within the shower area must be *waterproof* (see Figure 10.2.2).
   e. Penetrations within the *shower area* must be *waterproof*.
2. A shower with a *preformed shower base* must also comply with the requirements of (1), except for (a) which is not applicable.

PYRMONT CERTIFIERS
Pyrmont Certifiers Pty Ltd
RBC00045
Registered Certifier
APPROVED
Reference: 260258/01
Date: 10/06/2026

Figure 10.2.2: Extent of treatment for shower areas - concrete compressed fibre-cement and fibre-cement sheet floors.

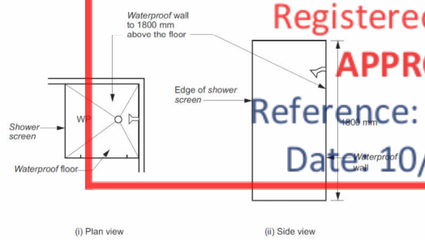

(a) Enclosed shower

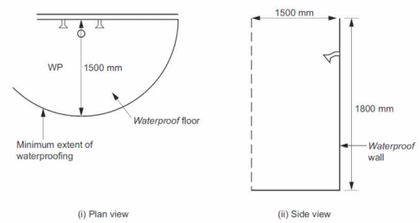

(b) Unenclosed shower

Figure Notes
Wall/floor junction heights are to be as per 10.2.2 to 10.2.6 (as applicable).

Notes
Where a shower is above a bath or spa, use requirements for shower.


10.2.3 Area outside shower area

1. For concrete, compressed fibre-cement and fibre-cement sheet flooring, the floor of the room must be water resistant.
2. For timber floors including particleboard, plywood and other timber based flooring materials, the floor of the room must be waterproof.
3. Wall/floor junctions must be -
   a. waterproof, and
   b. where a flashing is used, the horizontal leg must be not less than 40 mm.

10.2.4 Areas adjacent to baths and spas without showers

1. For areas adjacent to all baths and spas, the following applies:
   a. For concrete, compressed fibre-cement and fibre-cement sheet flooring, the floor of the room must be water resistant.
   b. For timber floors including particleboard, plywood and other timber based flooring materials, the floor of the room must be waterproof.
   c. Tap and spout penetrations must be waterproof where they occur in horizontal surfaces.
2. For areas adjacent to non-freestanding baths and spas, the following applies:
   a. Walls must be water resistant (see Figure 10.2.4a and Figure 10.2.4b)-
      • to a height of not less than 150mm above the vessel, for the extent of the vessel, where the vessel is within 75mm of a wall; and
      • for all exposed surfaces below vessel lip.
   b. Wall junctions and joints must be water resistant within 150mm above a vessel for the extent of the vessel.
   c. Wall/floor junctions must be waterproof for the extent of the vessel (see Figure 10.2.4a and Figure 10.2.4b).
3. For inserted baths and spas, the following applies.
   a. For floors and horizontal surfaces:
      • Any shelf area adjoining the bath or spa must be waterproof and include a waterstop under the vessel lip.
      • There are no requirements for the floor under a bath or spa.
   b. For walls:
      • Waterproof to not less than 150mm above the lip of a bath or spa.
      • There are no requirements for the floor under a bath or spa.
   c. For wall junctions and joints, the following applies:
      • Waterproof junctions within 150mm of a bath or spa.
      • There are no requirements for junctions and joints in walls beneath the lip of a bath or spa.
   d. Tap and spout penetrations must be waterproof where they occur in horizontal surfaces.

Figure 10.2.4a: Areas adjacent to baths and spas without showers for concrete, compressed fibre-cement and fibre-cement sheet flooring

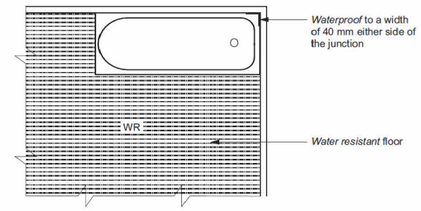



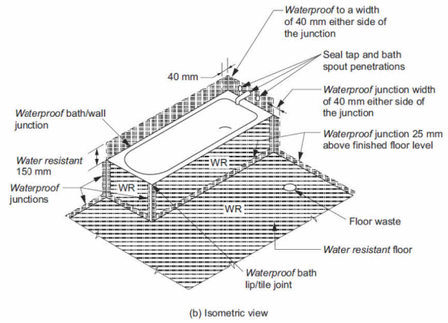


Figure 10.2.4b: Areas adjacent to baths and spas without showers for timber floors including particle-board, plywood and other floor materials

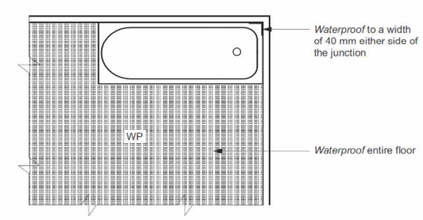


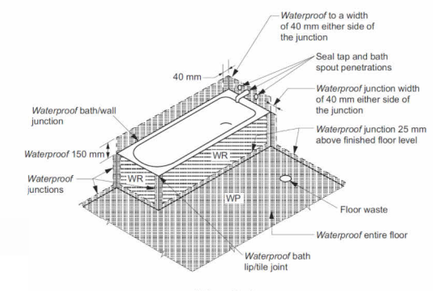

10.2.5 Other areas

1. For walls adjoining other types of vessels (e.g. sink, basin or laundry tub), the following applies:
   a. Walls must be water resistant to a height of not less than 150mm above the vessel, for the extent of the vessel, where the vessel is withing 75 mm of a wall (see Figure 10.2.5.)
   b. Waterproof wall junctions where a vessel is fixed to a wall.
   c. Waterproof tap and spout penetrations where they occur in surfaces required to be waterproof or water resistant.
2. For laundries and WCs, the following applies:
   a. The floor of the room must be water resistant.
   b. Wall/floor junctions must be water resistant, and where a flashing is used, the horizontal leg must not be less than 40 mm.
3. For WCs with handheld bidet spray installations, the following applies:
   a. The floor of the room must be waterproof.
   b. Walls must be -
      • waterproof in WC area within a 900 mm radius from the wall connection of the handheld bidet spray device to a height of not less than 150mm above the floor substrate; and
      • water resistant in WC area within a 900 mm radius from the wall connection of the handheld bidet device to not less than 1200 mm above the finished floor level of the WC.
   c. Wall junctions within the WC area within 900 mm radius from the wall connection of the handheld bidet spray device must be waterproof.
   d. Wall/floor junctions within the WC area within 1000 mm radius from the wall connection of the handheld bidet spray device must be waterproof.
   e. Penetrations in the WC area must be waterproof.

Figure 10.2.5: Bath and vessel abutting wall - areas to be protected

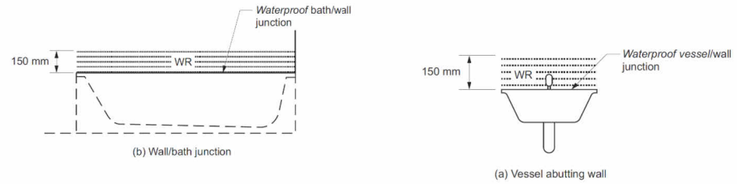

10.2.6 Waterproofing systems

1. For the purposes of this Part, a waterproofing system is deemed -
   a. waterproof, if it complies with (2); or
   b. water resistant, if it complies with (3).
2. For a waterproofing system required to be waterproof in accordance with 10.2.2 to 10.2.5, the materials nominated in 10.2.8 must be used.
3. For a waterproofing system required to be water resistant in accordance with 10.2.2 to 10.2.5, the materials nominated in 10.2.9 must be used in conjunction with the materials in 10.2.10.

10.2.12 Construction of wet area floors - falls

Where a floor waste is installed -
   a. the minimum continuous fall of a floor plane to the waste must be 1:80; and
   b. the maximum continuous fall of a floor plane to the waste must be 1:50.

CC ISSUE

REV	DATE	DESCRIPTION	BY
1	28-04-2026	Revision 1	

THIS DRAWING IS THE EXCLUSIVE PROPERTY OF THE DEVELOPER & THE REPRODUCTION OF ANY PART WITHOUT THE PRIOR WRITTEN CONSENT OF THE DEVELOPER IS A VIOLATION OF APPLICABLE LAWS. IN NO EVENT SHALL THE DEVELOPER BE HELD LIABLE FOR SPECIAL COLLATERAL, INCIDENTAL OR CONSEQUENTIAL LIABILITY IN CONNECTION WITH THE USE OF THIS DIGITAL DATA ONCE RELEASED FROM THE DEVELOPER'S OFFICE. THIS DRAWING IS TO BE READ & UNDERSTOOD IN CONJUNCTION WITH THE STRUCTURAL, MECHANICAL, ELECTRICAL & / OR ANY OTHER CONSULTANT'S DOCUMENTATION AS MAY BE APPLICABLE TO THE PROJECT PRIOR TO THE START OF ANY WORKS AND FOR ITS DURATION.

RUBY HOMES

PROJECT:
52 DRINKWATER AVENUE
LOT 42 52 DRINKWATER AVENUE ROUSE HILL

DRAWING TITLE:
WATERPROOFING DETAILS

NORTH:

LOT NO:	DATE:	SCALE:	DRAWING No:	REV:
42	22-05-2024	1 : 50	CC.18	1
DRAWN BY: AS	CHECKED BY: RH			ISSUED BY:
DRAFTED BY: SL	CLIENT NAME: Owner			

A3