


Fire separating wall to commence at footings and continue to the underside of the roof sheeting. No penetrations/attachments are permitted on the fire separating wall. The wall is to comply with the manufacturer's specifications and DTS provisions of Part 9.2 & 9.3 of the NCC Vol 2 – 2022 achieving a FRL 60/60/60 and performance requirement H3D1 of NCC vol.2 2022. Furthermore, the sound insulation of the Separating Wall complies with the DTS provisions of Part 10.7 of the NCC Vol 2 – 2022 and performance requirement H4D8 2022 vol.2

THE HILLS SHIRE COUNCIL

APPROVED
DEVELOPMENT CONSENT
101/2027/LD

Please refer to conditions of Development Consent
for details of matters which must be
complied with.

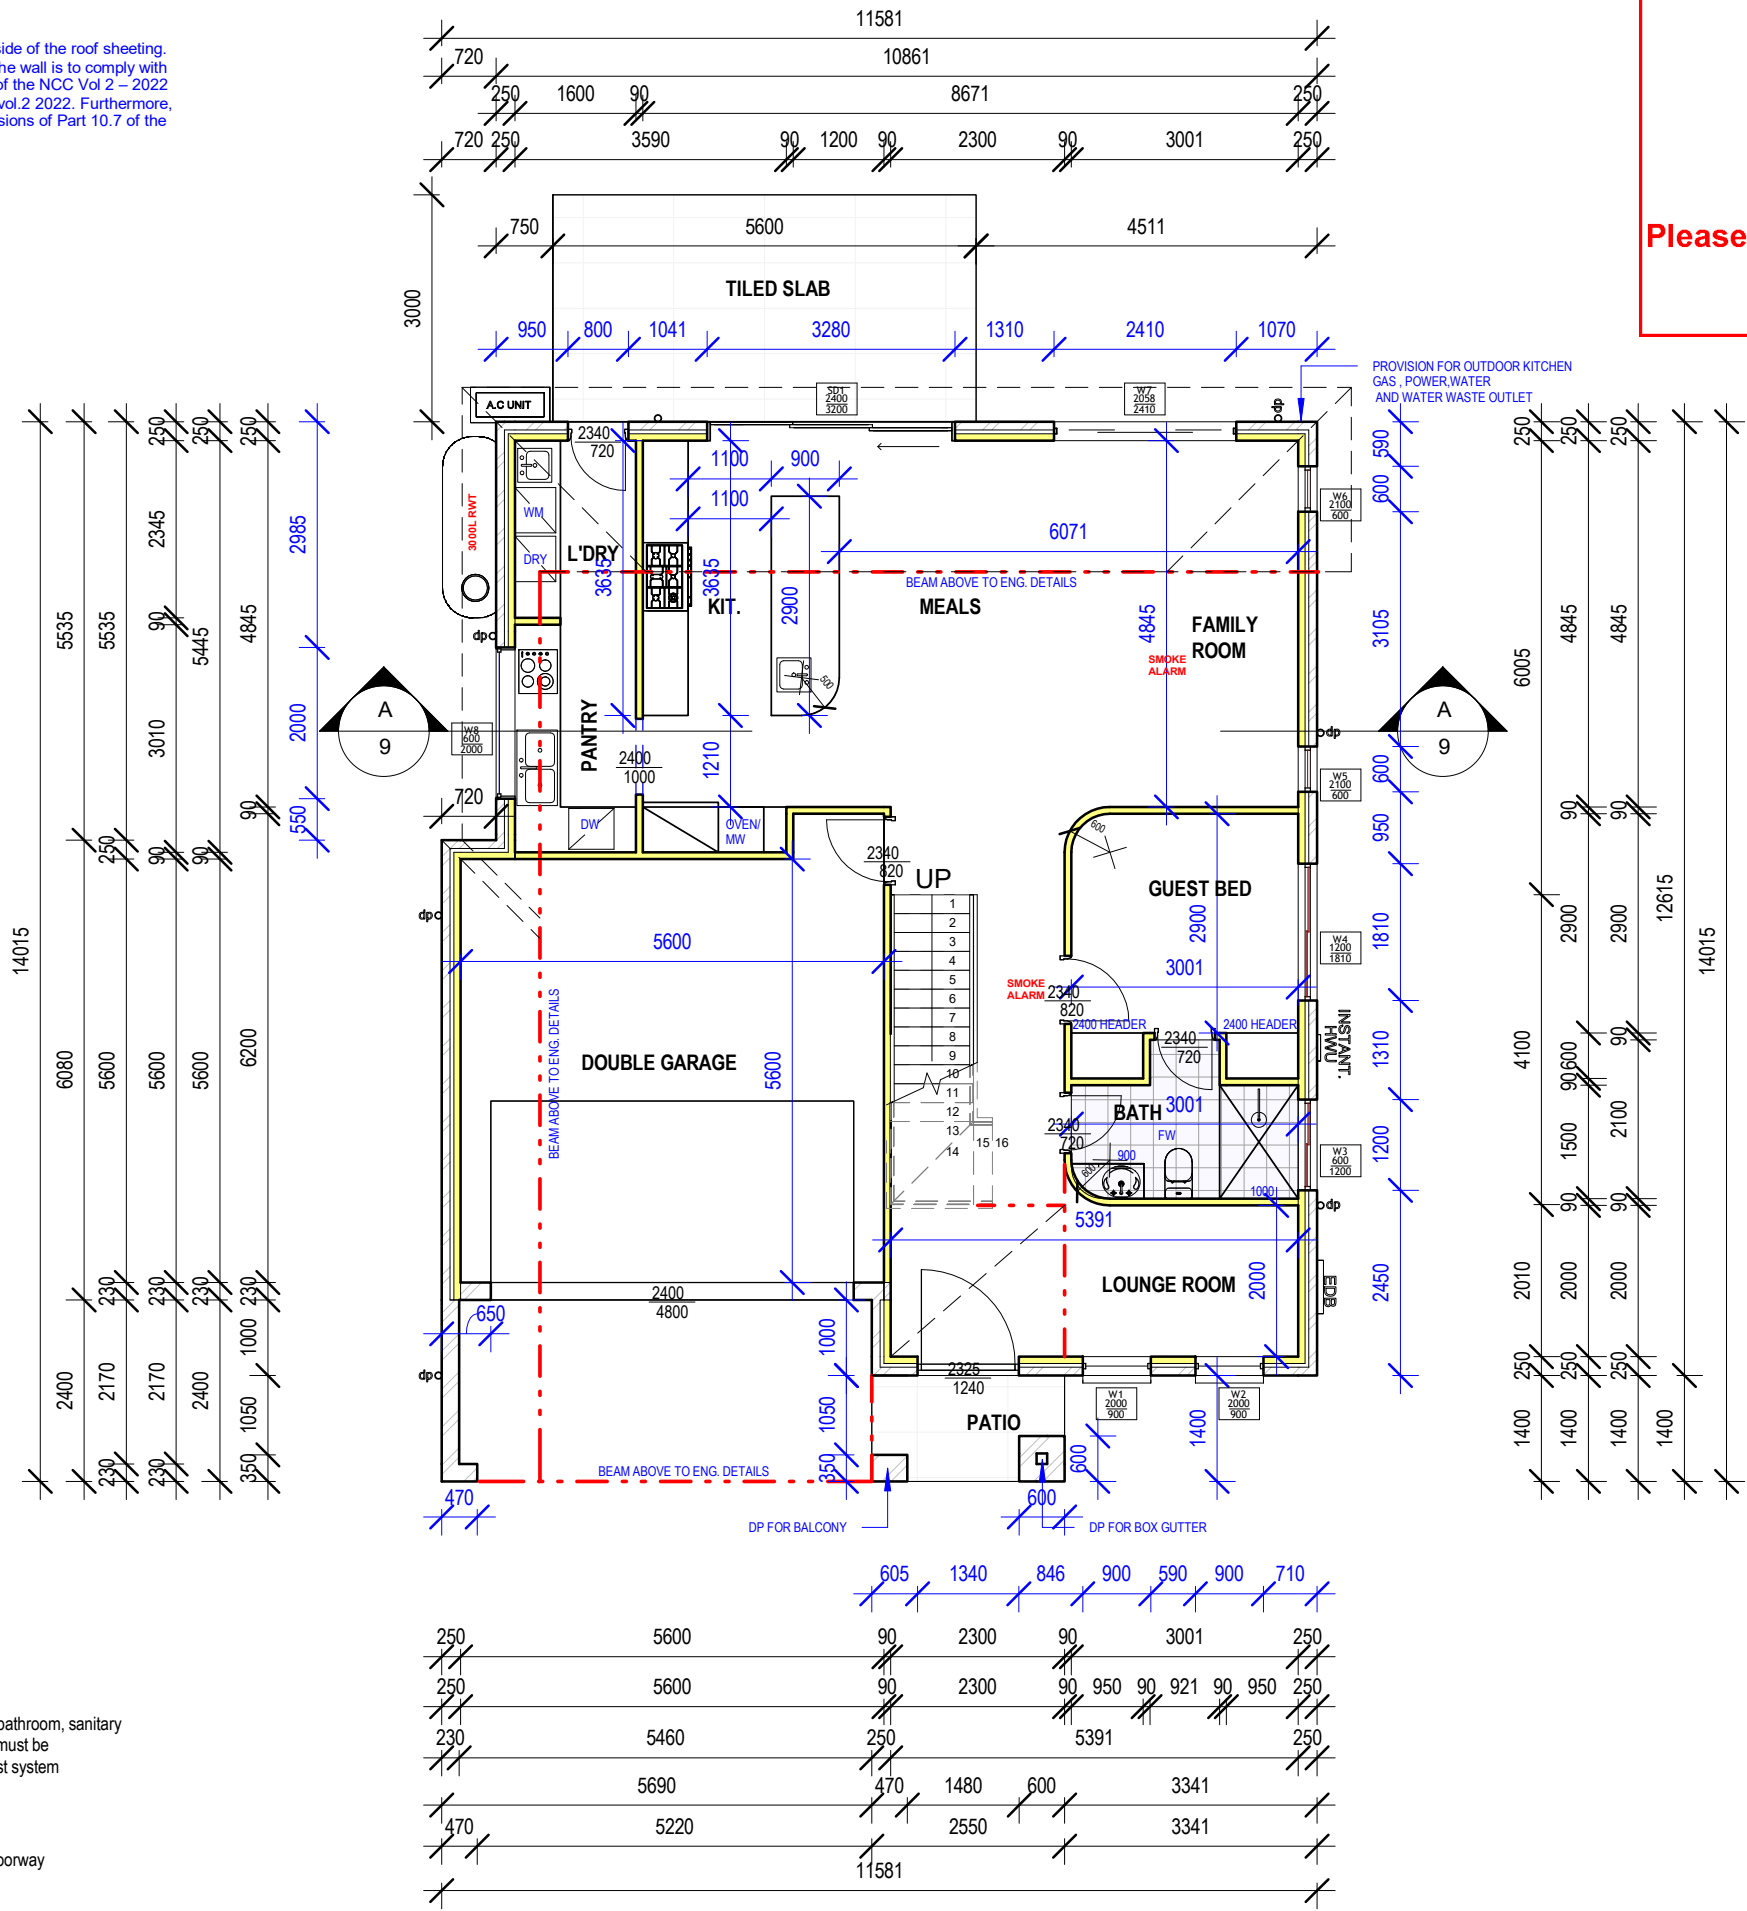

Fall to floor waste to be minimum 1:80 to maximum 1:50.

Mechanical ventilation to be provide on all bathrooms. Exhaust from a bathroom, sanitary compartment to discharge directly to outdoor air. This exhaust system must be interlocked with light switch and include run-on timer so that the exhaust system continues to operate for 10 minutes after the light switch is off.

note:
bathroom windows to have obscure glazing
install lift off door hinges where the closet pan is less than 1.2m from doorway

Mechanical ventilation to external for all laundry, W/C and kitchen

GROUND FLOOR PLAN



'ALL DIMENSIONS, LEVELS ,AREAS
AND DRAWINGS SHALL BE CHECKED
AND VERIFIED ON SITE BEFORE
APPROVAL,FABRICATION AND
START OF WORK'

CLIENT TUSHAR

JOB RESIDENCE

TITLE: DA -REVIEW

DATE:
09/07/26

SHEET:
2

ADDRESS 22 SCENERY ST - BOX HILL

DWG 2674

SCALE:
1 : 100

BY:
KV

REV.

No Date Description By
TJK DESIGN
RESIDENTIAL - COMMERCIAL - INDUSTRIAL
E: tim@tjkdesign.com.au ph: 0400035512



Certificate No. #HR-QBRK0K-01

Scan QR code or follow website link for rating details.

Assessor name

Caroline Newman

Accreditation No.

DMN/25/2280

Property Address

22, Scenery Street, BOX HILL,
NSW, 2765




http://www.hero-software.com.au/pdf/HR-QBRK0K-01



THE HILLS SHIRE COUNCIL

APPROVED
DEVELOPMENT CONSENT
101/2027/LD

Please refer to conditions of Development Consent
for details of matters which must be
complied with.

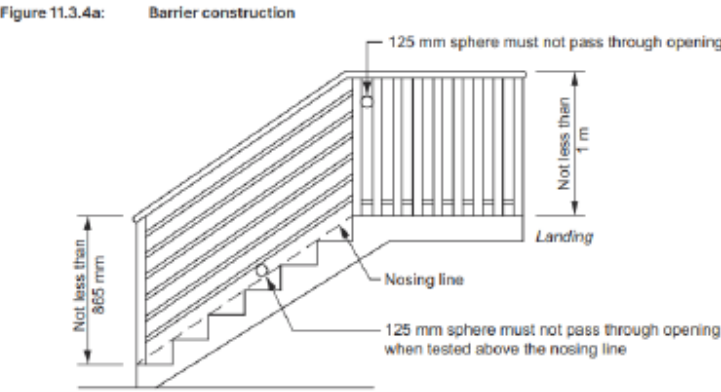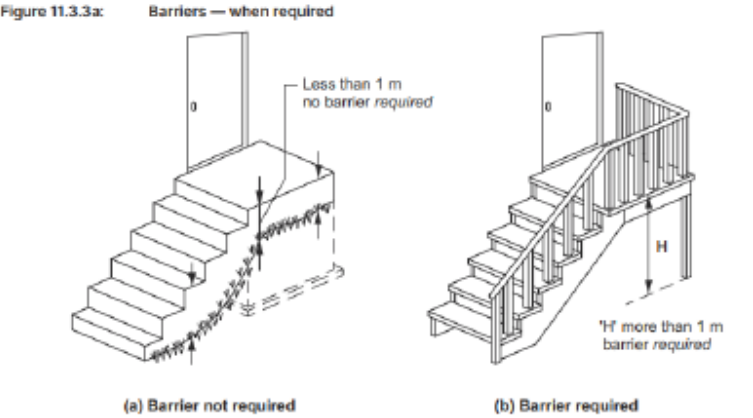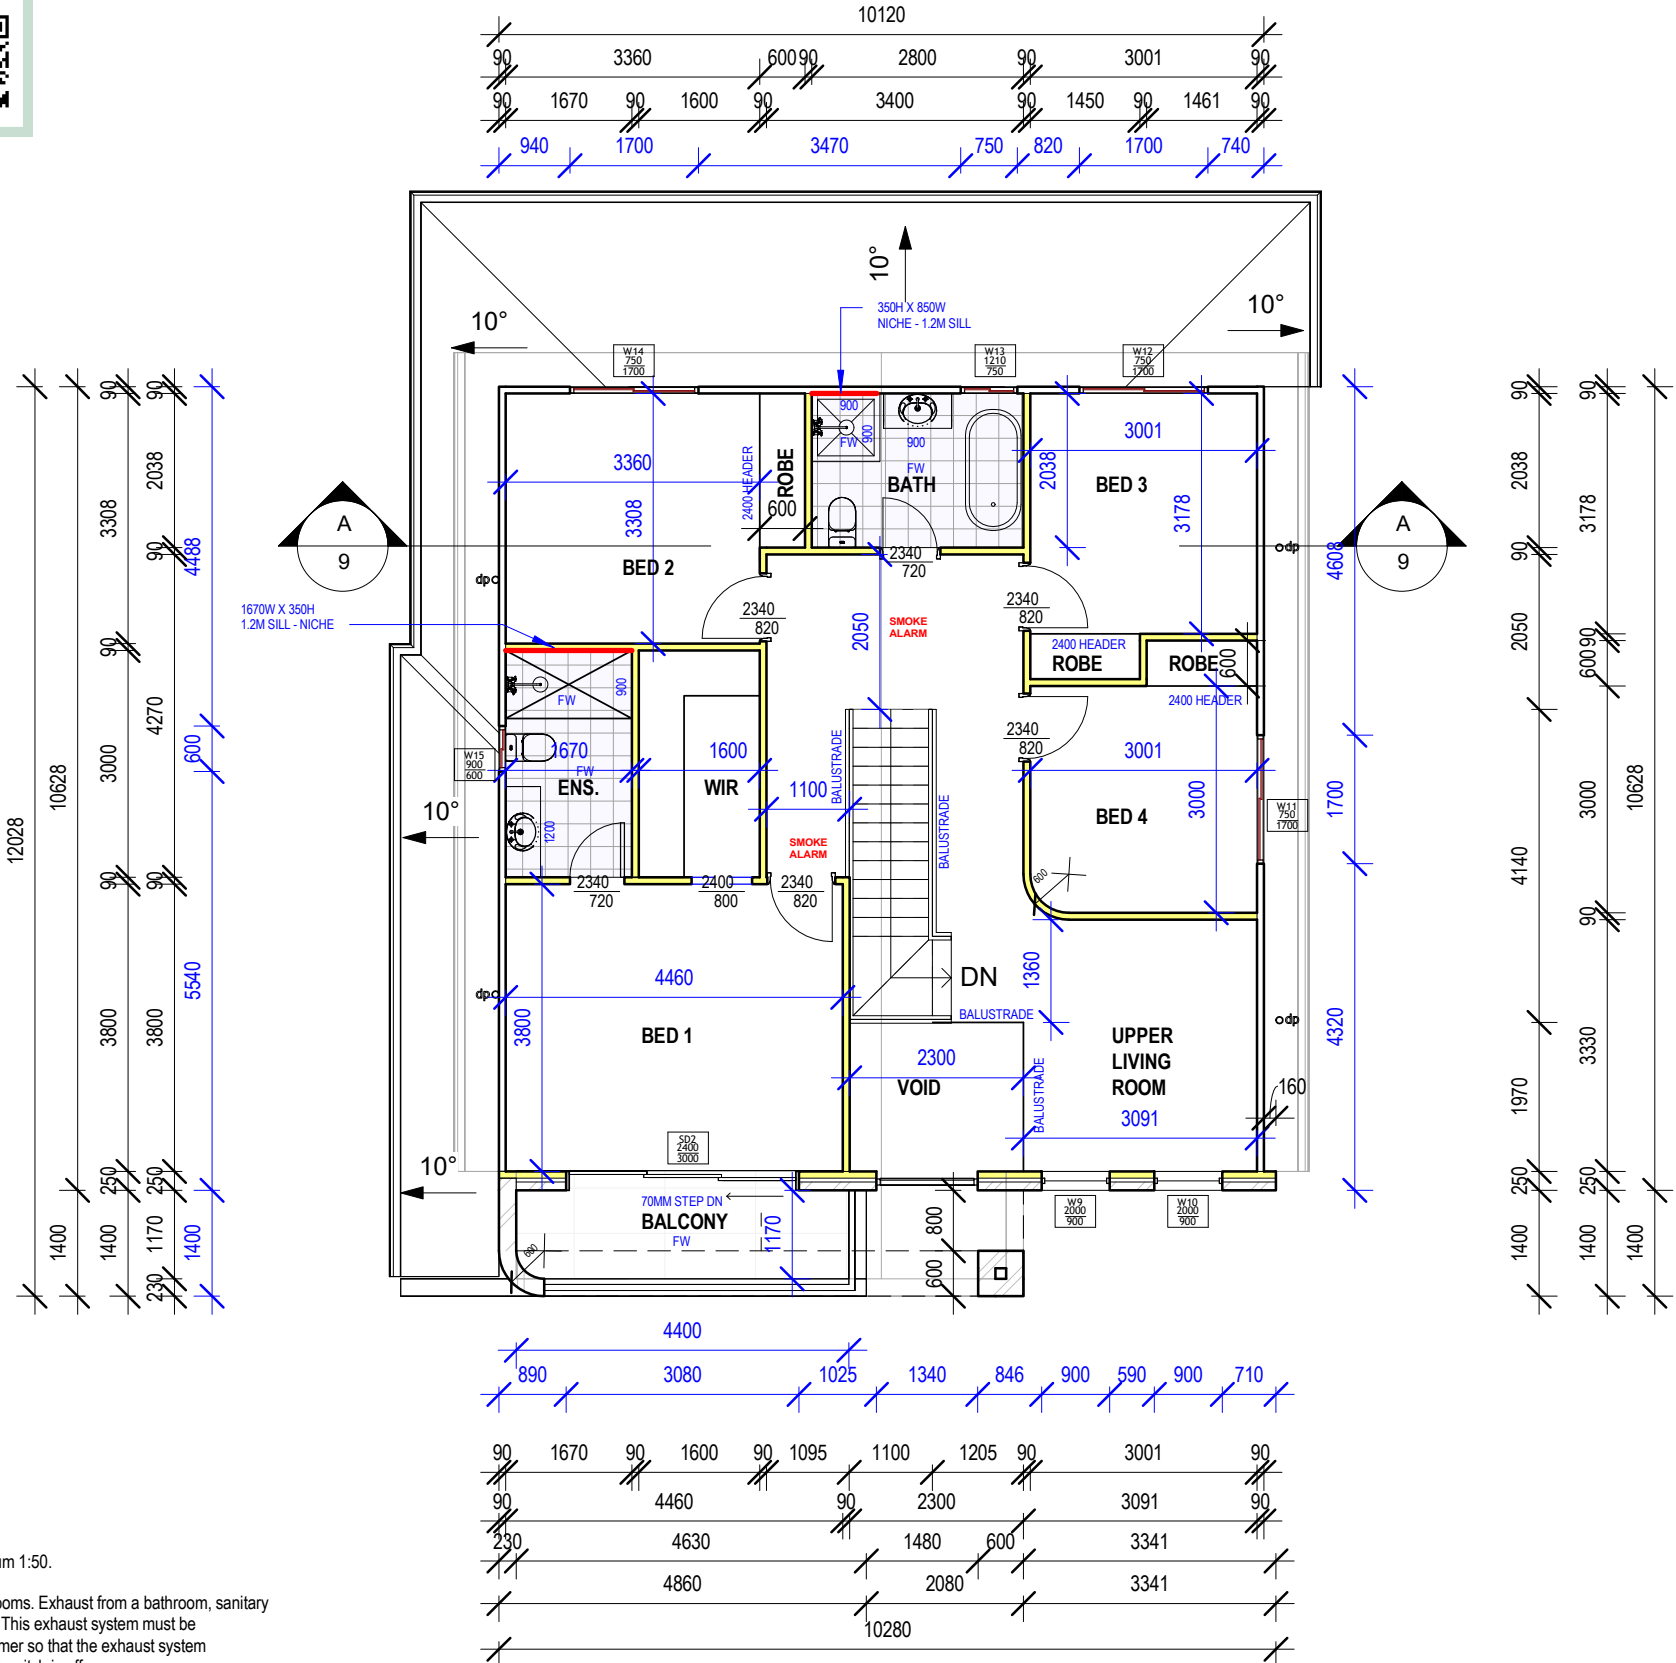

BALUSTRADE AND STAIRS TO COMPLY WITH PART 11.3 OF HOUSING
PROVISIONS NCC 2022

FIRST FLOOR PLAN

Fall to floor waste to be minimum 1:80 to maximum 1:50.

Mechanical ventilation to be provide on all bathrooms. Exhaust from a bathroom, sanitary compartment to discharge directly to outdoor air. This exhaust system must be interlocked with light switch and include run-on timer so that the exhaust system continues to operate for 10 minutes after the light switch is off.

note:
bathroom windows to have obscure glazing
install lift off door hinges where the closet pan is less than 1.2m from doorway

Mechanical ventilation to external for all laundry, W/C and kitchen

Balustrades to be min 1m high from the finished floor level

'ALL DIMENSIONS, LEVELS ,AREAS
AND DRAWINGS SHALL BE CHECKED
AND VERIFIED ON SITE BEFORE
APPROVAL,FABRICATION AND
START OF WORK'

CLIENT TUSHAR

ADDRESS 22 SCENERY ST - BOX HILL

JOB RESIDENCE

TITLE: DA -REVIEW

DWG 2674

SCALE:
1 : 100

DATE:
09/07/26

BY:
KV

SHEET:
3

REV.

No Date Description By

TJK DESIGN

RESIDENTIAL - COMMERCIAL -INDUSTRIAL

E: tim@tjkdesign.com.au ph: 0400035512