

HOMECERTS PTY LTD
Reference: 26235/01
Date: 29/05/2026
Construction Certificate (CC)
Dipak Ram
BDC 2686

 homecerts

NEW 1.2M FENCE ALONG
FRONT BOUNDARY

PROPOSED DRIVEWAY
CROSSOVER SUBJECT
TO COUNCIL APPROVAL

15 WIDE & VAR.
BITUMEN

43
D.P.773717

ROOF COLOUR TO BE
MEDIUM (SOLAR
ABSORPTANCE 0.48 - 0.5)

CLOTHES DRYING AREA OF
AT LEAST 16 LINEAL
METRES OF CLOTHES LINE

NEW 1.8M FENCE ALONG SIDE
AND REAR BOUNDARIES

ABOVE GROUND OSD BASIN 1
CAPACITY = 7.14M³
BASIN AREA = 46.16M²
MAX PONDING DEPTH = 0.2M
BASIN IL = 156.90
ORIFICE CL = 156.30
TWL = 157.10

SITE PLAN & ROOF PLAN, SITE ANALYSIS PLAN

1
A01.03

1 : 200

BASIX™ Certificate

Building Sustainability Index
www.planningportal.nsw.gov.au/development-and-assessment/basix

Single Dwelling

Certificate number: 1769660S_03

This certificate confirms that the proposed development will meet the NSW government's requirements for sustainability, if it is built in accordance with the commitments set out below. Terms used in this certificate, or in the commitments, have the meaning given by the document entitled "BASIX Definitions" dated 10/09/2020 published by the Department. This document is available at www.planningportal.nsw.gov.au/definitions

Secretary
Date of issue: Friday, 20 March 2026
To be valid, this certificate must be submitted with a development application or lodged with a complying development certificate application within 3 months of the date of issue.



When submitting this BASIX certificate with a development application or complying development certificate application, it must be accompanied by NatHERS certificate XND632KOL9.

Project summary		
Project name	3 Windsor Court, Castle Hill_03	
Street address	3 WINDSOR Court CASTLE HILL 2154	
Local Government Area	Hornsby Shire Council	
Plan type and plan number	Deposited Plan DP786466	
Lot no.	92	
Section no.	-	
Project type	dwelling house (detached)	
No. of bedrooms	5	
Project score		
Water	✔ 44	Target 40
Thermal Performance	✔ Pass	Target Pass
Energy	✔ 72	Target 72
Materials	✔ -50	Target n/a

CC Plans to comply with
the recommendations
from the arborist as
mentioned in the Arborist
Report prepared by
Growing My Way Tree
Consultants dated
January 2025

LEGEND:

-  SITE BOUNDARY
-  PROPOSED GROUND FLOOR OUTLINE
-  PROPOSED FIRST FLOOR OUTLINE
-  EXISTING EASEMENT

Certificate Prepared by	
Name / Company Name:	ecomaxhomes
ABN (if applicable):	22805208126

NOTES:
1. ALL DIMENSIONS AND FLOOR AREAS TO BE VERIFIED PRIOR TO THE COMMENCEMENT OF ANY BUILDING WORK
2. ANY DISCREPANCIES ARE TO BE CONFIRMED BY THE DESIGNER
3. LEVELS SHOWN ARE APPROXIMATE UNLESS ACCOMPANIED BY REDUCED LEVELS BY A REGISTERED SURVEYOR
4. FIGURED DIMENSIONS ARE TO BE TAKEN IN PREFERENCE TO SCALING
5. ALL BOUNDARY CLEARANCE MUST BE VERIFIED BY THE SURVEYOR PRIOR TO THE COMMENCEMENT OF ANY BUILDING WORK
6. WHERE ENGINEERING OR HYDRAULIC DRAWINGS ARE REQUIRED, SUCH MUST TAKE PREFERENCE TO THIS DRAWING
7. STORMWATER TO BE CONNECTED AND DISCHARGED TO COUNCIL'S REQUIREMENTS AND TO AS 3500.3
8. ALL SERVICES TO BE LOCATED AND VERIFIED BY THE BUILDER WITH THE RELEVANT AUTHORITIES PRIOR TO THE COMMENCEMENT OF ANY BUILDING.

ADDRESS:
**3 WINDSOR CT CASTLE HILL (LOT 1)
LOT 92 DP 786466**
CLIENT:
MR. REHAN FIROZ & MR.SALMAN FIROZ

B	REVISION	14-05-2026
A	ISSUED FOR CC	08-02-2026
ISSUE	REVISION	DATE

ISSUE:

B

CHECKED BY: D.NOBEL
DRAWN BY: A.PERVAIZ

TRUE NORTH:




DRAWING TITLE:
**SITE PLAN & ROOF PLAN, SITE ANALYSIS
PLAN**

DRAWING NUMBER: A01.03
SCALE: 1 : 200 @ A3



ABN: 51 463 906 127
UNIT 1/128-130 VICTORIA STREET WERRINGTON NSW 2747
0431231255, info@adadesign.com.au
NOMINATED ARCHITECT: DENIS NOBEL (REG.12432)

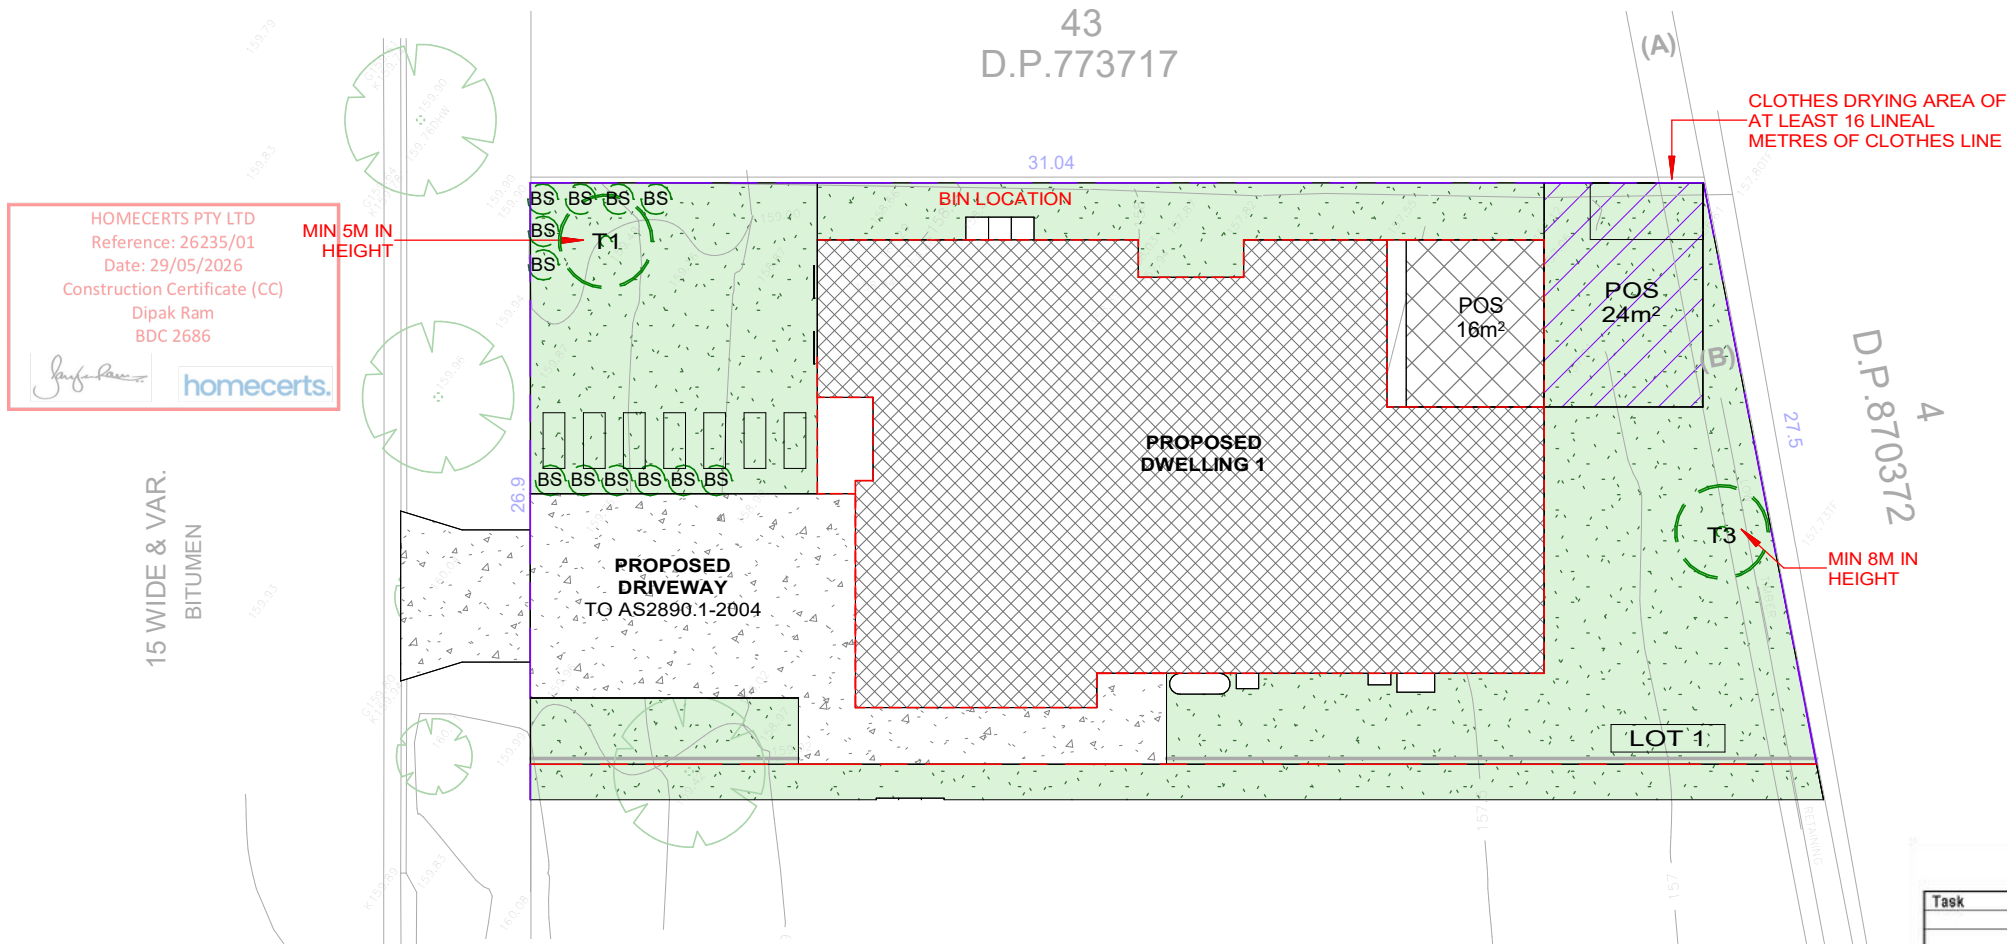

LEGEND:

SITE BOUNDARY

PROPOSED DWELLING

PROPOSED DRIVEWAY & CONCRETE AREAS

PROPOSED LANDSCAPING

MIN. POS 24m²

EXISTING EASEMENT

BS

PROPOSED SHRUB
Bursaria Spinosa (Blacktorn) 1m

T1-2

PROPOSED TREE
ACACIA BINERVIA (*Myall Wattle*) 5m
SIZE: MIN. 75 LTR

T3-4

PROPOSED TREE
ACACIA BINERVIA (*Myall Wattle*) 8m
SIZE: MIN. 75 LTR


NOTES:
MIN 50% OF THE OVERALL NUMBER OF TREES & SHRUBS SHOULD BE NATIVE TO THIS REGION

1

A01.05



LANDSCAPE PLAN

1 : 200

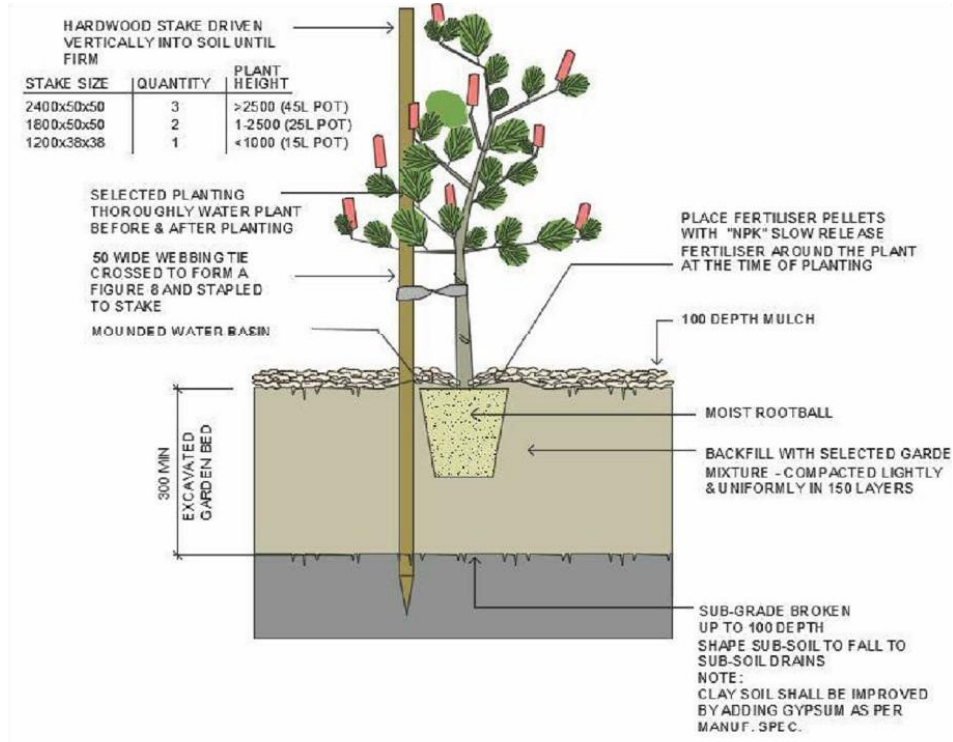

2. TREE & SHRUB PLANTING IN GARDEN BED

NOTE:
DO NOT PLANT IN UNSUITABLE WEATHER CONDITIONS SUCH AS EXTREME HEAT, COLD, WIND OR RAIN
CLAY SOIL IS TO BE TREATED WITH CLAY BREAKER AND ORGANIC COMPOST

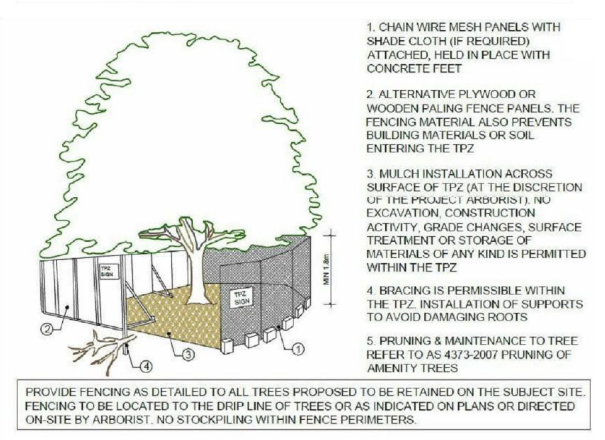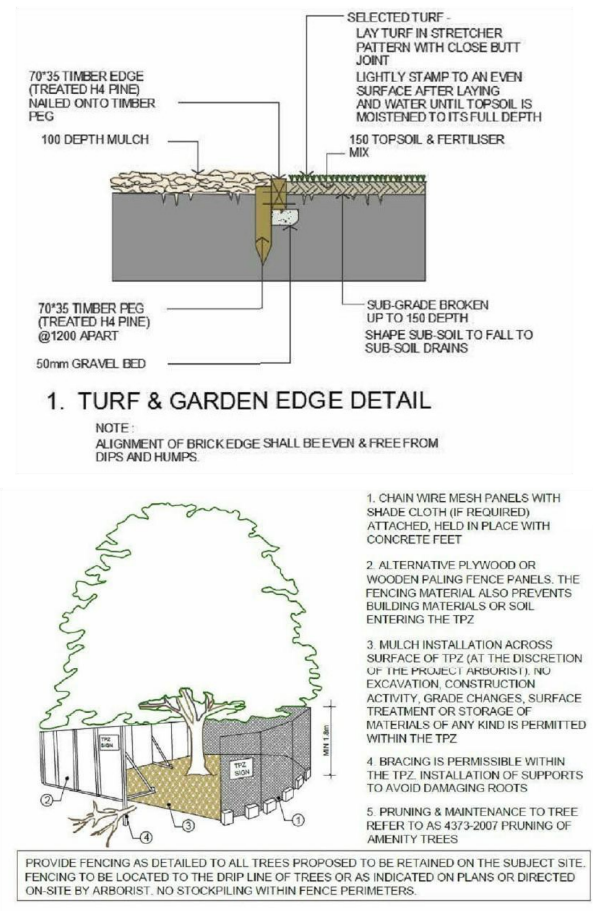

LANDSCAPE MAINTENANCE SCHEDULE

Task	MONTH	JAN	FEB	MAR	APR	MAY	JUNE	JULY	AUG	SEPT	OCT	NOV	DEC
CARE OF PLANTS													
Monitoring													
Pruning (if needed)													
Deadhead plants													
Fertilization													
Cut back perennials & grasses													
Watering - as needed													
PLANTING BEDS													
Edging													
Weeding - as needed													
Mulching													
Soil testing													
Leaf Removal (if needed)													
PEST MANAGEMENT													
Monitoring													
LAWNS													
Fertilize/Lime													
Seeding													
WINTER CLEAN UP													
SNOW REMOVAL PLAN													

2. Minimum soil standards for plant sizes are provided in accordance with the Table below.

Tree Size	Height	Spread	Min Soil Area	Min soil depth
Large trees	>12m	>8m	10 x 10m	1200mm
Medium trees	8-12m	4-8m	6 x 6m	1000mm
Small trees	5-8m	<4m	3.5 x 3.5m	800mm
Shrubs	-	-	n/a	500-600mm
Groundcover	-	-	n/a	300-450mm
Turf	-	-	n/a	200mm

NOTES:
1. ALL DIMENSIONS AND FLOOR AREAS TO BE VERIFIED PRIOR TO THE COMMENCEMENT OF ANY BUILDING WORK
2. ANY DISCREPANCIES ARE TO BE CONFIRMED BY THE DESIGNER
3. LEVELS SHOWN ARE APPROXIMATE UNLESS ACCOMPANIED BY REDUCED LEVELS BY A REGISTERED SURVEYOR
4. FIGURED DIMENSIONS ARE TO BE TAKEN IN PREFERENCE TO SCALING
5. ALL BOUNDARY CLEARANCE MUST BE VERIFIED BY THE SURVEYOR PRIOR TO THE COMMENCEMENT OF ANY BUILDING WORK
6. WHERE ENGINEERING OR HYDRAULIC DRAWINGS ARE REQUIRED, SUCH MUST TAKE PREFERENCE TO THIS DRAWING
7. STORMWATER TO BE CONNECTED AND DISCHARGED TO COUNCIL'S REQUIREMENTS AND TO AS 3500.3
8. ALL SERVICES TO BE LOCATED AND VERIFIED BY THE BUILDER WITH THE RELEVANT AUTHORITIES PRIOR TO THE COMMENCEMENT OF ANY BUILDING.

ADDRESS:
3 WINDSOR CT CASTLE HILL (LOT 1)
LOT 92 DP 786466
CLIENT:
MR. REHAN FIROZ & MR.SALMAN FIROZ

B	REVISION	14-05-2026
A	ISSUED FOR CC	08-02-2026
ISSUE	REVISION	DATE

ISSUE:
B
CHECKED BY: D.NOBEL
DRAWN BY: A.PERVAIZ

TRUE NORTH:

DRAWING TITLE:
LANDSCAPE PLAN
DRAWING NUMBER:
A01.05
SCALE:
1 : 200 @ A3

ABN: 51 463 906 127
UNIT 1/128-130 VICTORIA STREET WERRINGTON NSW 2747
0431231255, info@adadesign.com.au
NOMINATED ARCHITECT: DENIS NOBEL (REG.12432)

HOMECERTS PTY LTD
Reference: 26235/01
Date: 29/05/2026
Construction Certificate (CC)
Dipak Ram
BDC 2686




FLOOR AREA CALCULATIONS	
LOT 1 - DW1:	
PROPOSED GROUND FLOOR (INTERNAL):	147.7m ²
PROPOSED FIRST FLOOR (INTERNAL):	120.7m ²
PROPOSED GARAGE (INTERNAL) AREA:	32.4m ²
PROPOSED PORCH AREA:	3.6m ²
PROPOSED ALFRESCO AREA:	18.3m ²
TOTAL AREA:	322.7m²
TOTAL AREA (EXCLUDING PORCH AND ALFRESCO):	300.8m²

- S** SMOKE ALARM SYSTEM
- MV** MECHANICAL VENTILATION
- FIRST FLOOR OUTLINE
- GROUND FLOOR OUTLINE

Note: Private EV connection of a minimum 15A circuit and power point to enable easy future EV connection in the garage connection to the main switch board.

1 A02 GROUND FLOOR PLAN

1 : 120

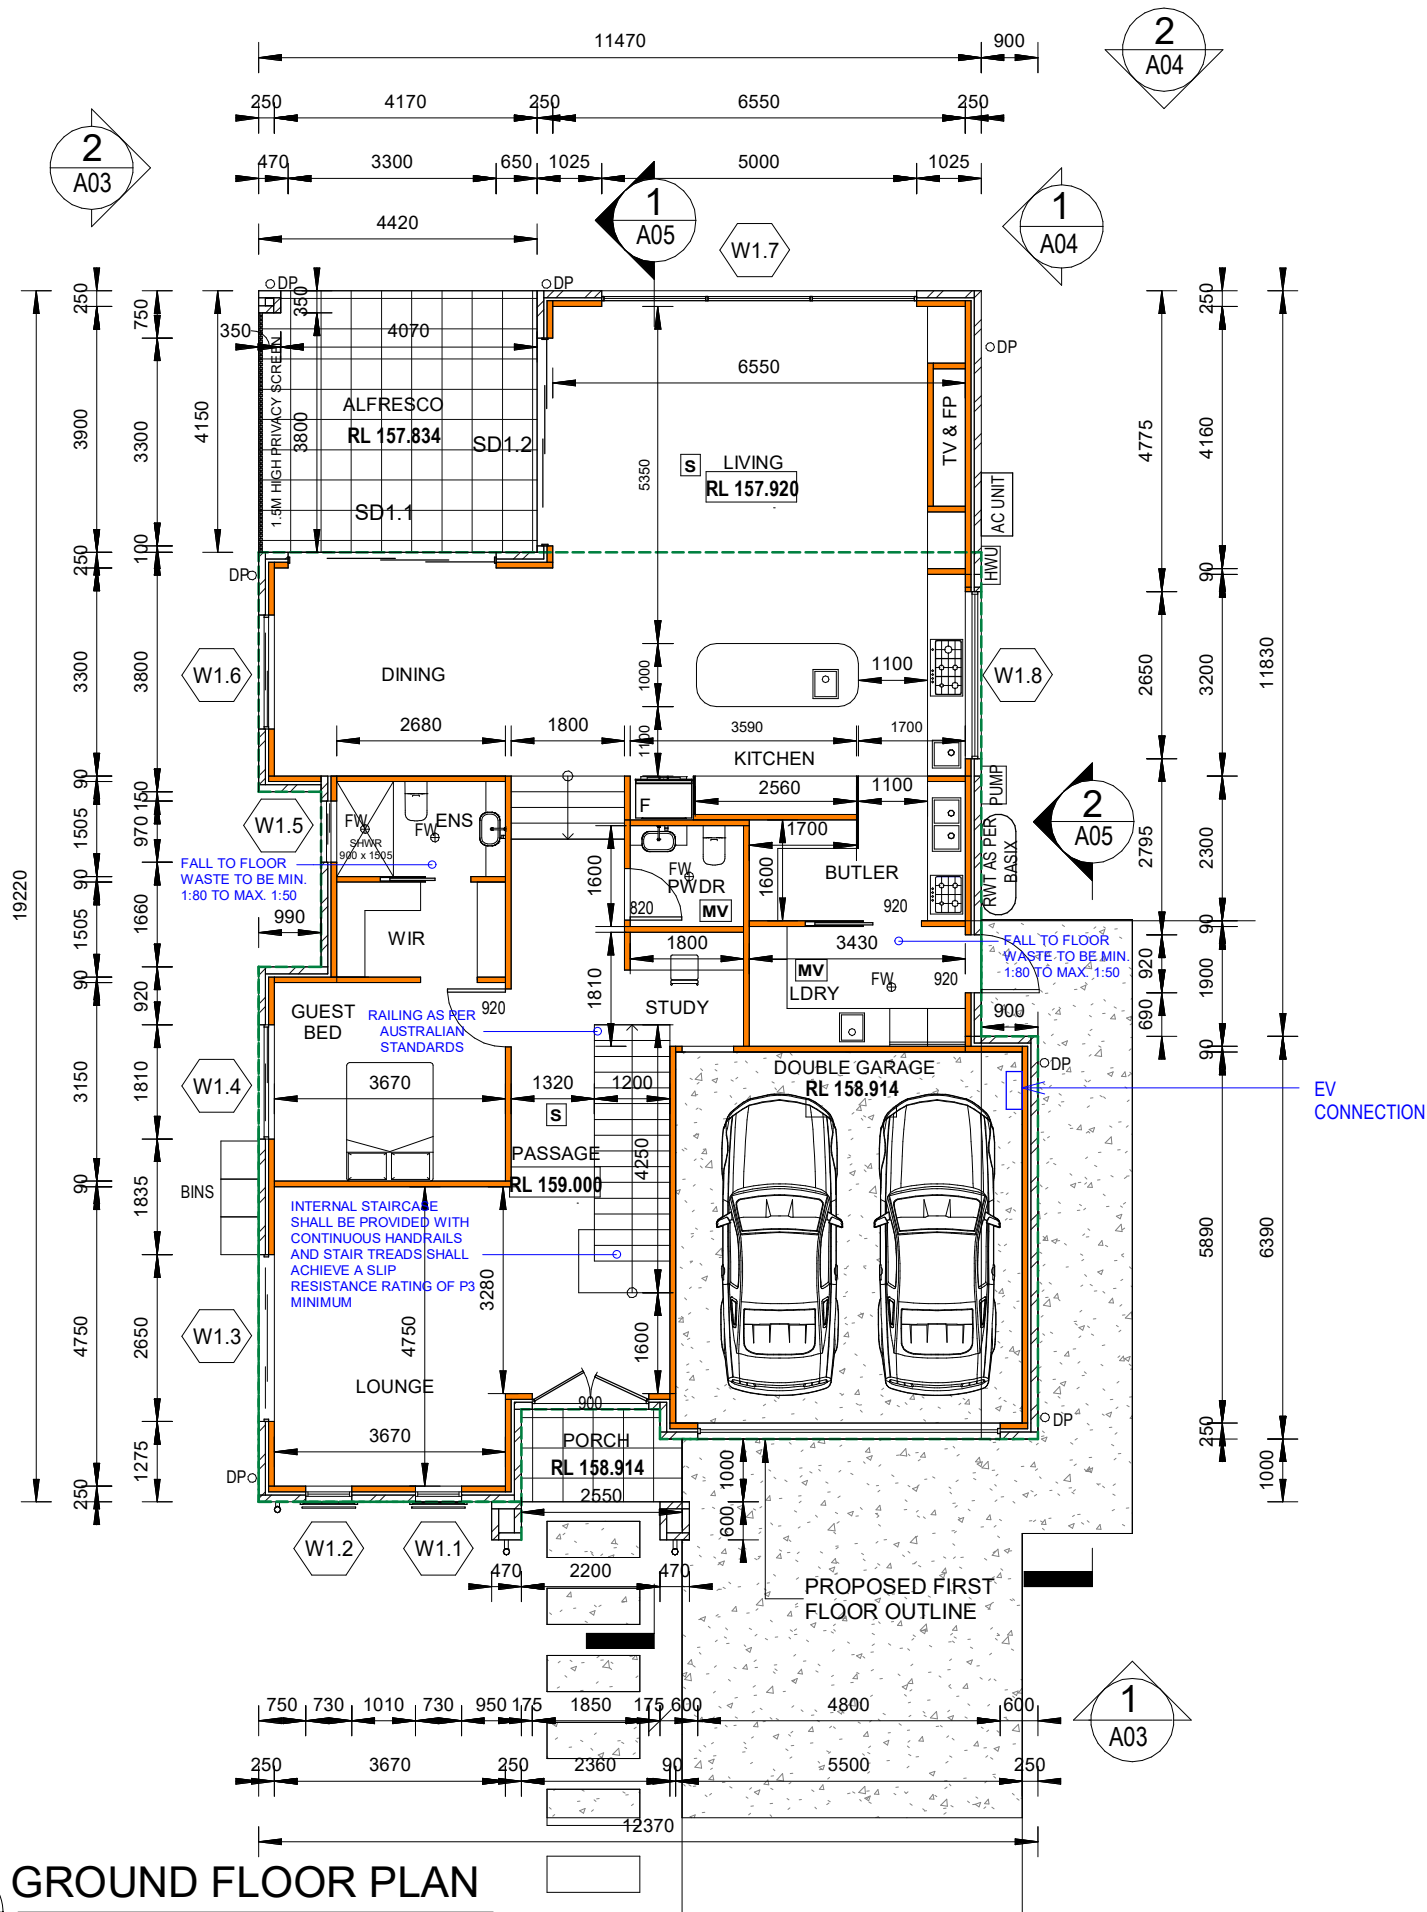

NOTE: WHERE FLOOR LEVEL IS >2M ABOVE EXTERNAL SURFACE BENEATH WINDOW, AND WHERE THE OPENABLE SASH IS <1.7M, ANY OPENABLE WINDOW IN A BEDROOM MUST BE RESTRICTED TO A 125MM OPENING. IN REGARDS TO OTHER ROOMS, THIS APPLIES WHERE THE FLOOR LEVEL IS >4M. **R** DENOTES **R**ESTRICTION ON THE WINDOW

NOTE: **L/O** DENOTES **L**IFT **O**FF HINGES TO ALL WET AREAS

NOTE: REQUIRED ARTIFICIAL FLUORESCENT LIGHTING AS PER BASIX CERTIFICATE

NO DOWNLIGHTS TO BE INSTALLED ON FIRST FLOOR CEILING UNLESS SPECIFIED

NOTE: MECHANICAL VENTILATION TO BATHROOMS, ENSUITES, WC, LAUNDRIES MUST BE DUCTED TO OUTSIDE AIR

NOTE: WET AREA MUST COMPLY WITH ONE OF THE FOLLOWING: AS3740-2021 OR NCC PART 10.2

NOTE: **F** DENOTES FIXED WINDOW

NOTE: ALL WINDOWS & DOORS TO BE COMMERCIAL GRADE

NOTE: ROOF VENTILATION SHALL COMPLY WITH CLAUSE 10.8 OF THE NCC

NOTE: WET AREA SHALL BE WATERPROOFED AS PER CLAUSE 10.2 OF THE NCC- PUDDLE FLANGES SHALL BE FLUSHED WITH THE STRUCTURAL FLOOR AND ADEQUATELY WATERPROOFED.

NCC 2022 - ABCB HOUSING PROVISIONS 10.8.3 VENTILATION OF ROOF SPACES:

ROOF SPACE AS PER 10.8.3(1)(a) & (b) TO BE PROVIDED AND VENTILATION TO ROOF SPACE REQUIRED AS PER 10.8.3(1)(c).

EXHAUST FROM A BATHROOM, SANITARY COMPARTMENT TO DISCHARGE DIRECTLY TO OUTDOOR AIR. THIS EXHAUST SYSTEM MUST BE INTERLOCKED WITH LIGHT SWITCH AND INCLUDE RUN-ON TIMER SO THAT THE EXHAUST SYSTEM CONTINUES TO OPERATE FOR 10 MINUTES AFTER THE LIGHT SWITCH IS OFF.

GYPROCK SHAFT LINER PARTY WALL: DESIGN/CONSTRUCTION ARE TO COMPLY WITH BCA CLAUSE 9.3 FOR FIRE SEPARATION AND CLAUSE 10.7 FOR SOUND INSULATION. SEPARATING WALL TO ACHIEVE A MINIMUM FRL OF 60/60/60 AND SOUND INSULATION OF \$R_w + C_{tr}\$ (AIRBORNE) NOT LESS THAN 50 AND DISCONTINUOUS CONSTRUCTION. GYPROCK FIRE-RATED SEPARATING WALL-CENTRAL FIRE BARRIER COMPRISING—25 MM GYPROCK SHAFT LINER PANEL SECURED WITHIN GALVANISED STEEL CHANNELS AND HELD BY ALUMINIUM CLIPS DESIGNED FOR FIRE-AWAY RELEASE. MINIMUM 20 MM CAVITY ON BOTH SIDES OF THE SHAFT LINER PANEL. 70 MM OR 90 MM STEEL OR TIMBER STUDS SET BACK FROM THE LINER PANEL TO ENSURE DISCONTINUITY. 75 MM THICK GLASS WOOL INSULATION (MIN. DENSITY 11 KG/M³) OR EQUIVALENT POLYESTER INSULATION WITHIN THE STUD CAVITIES. 1 LAYER OF 13 MM GYPROCK PLASTERBOARD (E.G., SOUNDCEK OR FIRECEK) TO THE EXTERNAL FACE OF EACH STUD WALL.

NOTES:

- ALL DIMENSIONS AND FLOOR AREAS TO BE VERIFIED PRIOR TO THE COMMENCEMENT OF ANY BUILDING WORK
- ANY DISCREPANCIES ARE TO BE CONFIRMED BY THE DESIGNER
- LEVELS SHOWN ARE APPROXIMATE UNLESS ACCOMPANIED BY REDUCED LEVELS BY A REGISTERED SURVEYOR
- FIGURED DIMENSIONS ARE TO BE TAKEN IN PREFERENCE TO SCALING
- ALL BOUNDARY CLEARANCE MUST BE VERIFIED BY THE SURVEYOR PRIOR TO THE COMMENCEMENT OF ANY BUILDING WORK
- WHERE ENGINEERING OR HYDRAULIC DRAWINGS ARE REQUIRED, SUCH MUST TAKE PREFERENCE TO THIS DRAWING
- STORMWATER TO BE CONNECTED AND DISCHARGED TO COUNCIL'S REQUIREMENTS AND TO AS 3500.3
- ALL SERVICES TO BE LOCATED AND VERIFIED BY THE BUILDER WITH THE RELEVANT AUTHORITIES PRIOR TO THE COMMENCEMENT OF ANY BUILDING.

ADDRESS:
3 WINDSOR CT CASTLE HILL (LOT 1)
LOT 92 DP 786466

CLIENT:
MR. REHAN FIROZ & MR.SALMAN FIROZ

REVISION		
B	REVISION	14-05-2026
A	ISSUED FOR CC	08-02-2026
ISSUE	REVISION	DATE

ISSUE: **B**

TRUE NORTH: 

CHECKED BY: D.NOBEL

DRAWN BY: A.PERVAIZ

DRAWING TITLE:
PROPOSED DWELLING 1 GROUND FLOOR PLAN

DRAWING NUMBER: **A02**

SCALE: **As indicated @ A3**

ADA
design

ABN: 51 463 906 127
UNIT 1/128-130 VICTORIA STREET WERRINGTON NSW 2747
0431231255, info@adadesign.com.au
NOMINATED ARCHITECT: DENIS NOBEL (REG.12432)

HOMECERTS PTY LTD
Reference: 26235/01
Date: 29/05/2026
Construction Certificate (CC)
Dipak Ram
BDC 2686



AS 3740:2021 CLAUSE 4.8.2
WATERSTOP FOR UNENCLOSED
SHOWERS - REFER TO TYPICAL
DETAIL SHEET

FALL TO FLOOR
WASTE TO BE MIN.
1:80 TO MAX. 1:50

- S

SMOKE ALARM SYSTEM
- MV

MECHANICAL VENTILATION
- FIRST FLOOR OUTLINE
- GROUND FLOOR OUTLINE

1
A02a

FIRST FLOOR PLAN

1 : 120

ADDRESS:
**3 WINDSOR CT CASTLE HILL (LOT 1)
LOT 92 DP 786466**

CLIENT:
MR. REHAN FIROZ & MR.SALMAN FIROZ

B	REVISION	14-05-2026
A	ISSUED FOR CC	08-02-2026
ISSUE	REVISION	DATE

ISSUE:
B

CHECKED BY: D.NOBEL
DRAWN BY: A.PERVAIZ

TRUE NORTH:


DRAWING TITLE:
**PROPOSED DWELLING 1 FIRST FLOOR
PLAN**

DRAWING NUMBER:
A02a

SCALE:
As indicated @ A3



ABN: 51 463 906 127
UNIT 1/128-130 VICTORIA STREET WERRINGTON NSW 2747
0431231255, info@adadesign.com.au
NOMINATED ARCHITECT: DENIS NOBEL (REG.12432)

NOTE: WHERE FLOOR LEVEL IS >2M ABOVE EXTERNAL SURFACE BENEATH WINDOW, AND WHERE THE OPENABLE SASH IS <1.7M, ANY OPENABLE WINDOW IN A BEDROOM MUST BE RESTRICTED TO A 125MM OPENING. IN REGARDS TO OTHER ROOMS, THIS APPLIES WHERE THE FLOOR LEVEL IS >4M. **R** DENOTES **R**ESTRICTION ON THE WINDOW

NOTE: **L/O** DENOTES **L**IFT **O**FF HINGES TO ALL WET AREAS

NOTE: REQUIRED ARTIFICIAL FLUORESCENT LIGHTING AS PER BASIX CERTIFICATE

NO DOWNLIGHTS TO BE INSTALLED ON FIRST FLOOR CEILING UNLESS SPECIFIED

NOTE: MECHANICAL VENTILATION TO BATHROOMS, ENSUITES, WC, LAUNDRIES MUST BE DUCTED TO OUTSIDE AIR

NOTE: WET AREA MUST COMPLY WITH ONE OF THE FOLLOWING:
AS3740-2021 OR NCC PART 10.2

NOTE: **F** DENOTES FIXED WINDOW

NOTE: ALL WINDOWS & DOORS TO BE COMMERCIAL GRADE

NOTE: ROOF VENTILATION SHALL COMPLY WITH CLAUSE 10.8 OF THE NCC

NOTE: WET AREA SHALL BE WATERPROOFED AS PER CLAUSE 10.2 OF THE NCC- PUDDLE FLANGES SHALL BE FLUSHED WITH THE STRUCTURAL FLOOR AND ADEQUATELY WATERPROOFED.

[NCC 2022 - ABCB HOUSING PROVISIONS 10.8.3 VENTILATION OF ROOF SPACES:](#)

ROOF SPACE AS PER 10.8.3(1)(a) & (b) TO BE PROVIDED AND VENTILATION TO ROOF SPACE REQUIRED AS PER 10.8.3(1)(c).

EXHAUST FROM A BATHROOM, SANITARY COMPARTMENT TO DISCHARGE DIRECTLY TO OUTDOOR AIR. THIS EXHAUST SYSTEM MUST BE INTERLOCKED WITH LIGHT SWITCH AND INCLUDE RUN-ON TIMER SO THAT THE EXHAUST SYSTEM CONTINUES TO OPERATE FOR 10 MINUTES AFTER THE LIGHT SWITCH IS OFF.

GYPROCK SHAFT LINER PARTY WALL: DESIGN/CONSTRUCTION ARE TO COMPLY WITH BCA CLAUSE 9.3 FOR FIRE SEPARATION AND CLAUSE 10.7 FOR SOUND INSULATION. SEPARATING WALL TO ACHIEVE A MINIMUM FRL OF 60/60/60 AND SOUND INSULATION OF \$R_w + C_{tr}\$ (AIRBORNE) NOT LESS THAN 50 AND DISCONTINUOUS CONSTRUCTION.GYPROCK FIRE-RATED SEPARATING WALL:CENTRAL FIRE BARRIER COMPRISING—25 MM GYPROCK SHAFT LINER PANEL SECURED WITHIN GALVANISED STEEL CHANNELS AND HELD BY ALUMINIUM CLIPS DESIGNED FOR FIRE-AWAY RELEASE.MINIMUM 20 MM CAVITY ON BOTH SIDES OF THE SHAFT LINER PANEL. 70 MM OR 90 MM STEEL OR TIMBER STUDS SET BACK FROM THE LINER PANEL TO ENSURE DISCONTINUITY.75 MM THICK GLASS WOOL INSULATION (MIN. DENSITY 11 KG/M³) OR EQUIVALENT POLYESTER INSULATION WITHIN THE STUD CAVITIES.1 LAYER OF 13 MM GYPROCK PLASTERBOARD (E.G., SOUNDCEK OR FIRECEK) TO THE EXTERNAL FACE OF EACH STUD WALL.


8.5M TO NGL

NOTE: WHERE FLOOR LEVEL IS >2M ABOVE EXTERNAL SURFACE BENEATH WINDOW, AND WHERE THE OPENABLE SASH IS <1.7M, ANY OPENABLE WINDOW IN A BEDROOM MUST BE RESTRICTED TO A 125MM OPENING.


IN REGARDS TO OTHER ROOMS, THIS APPLIES WHERE THE FLOOR LEVEL IS >4M. R DENOTES RESTRICTION ON THE WINDOW

Construction Certificate (CC)

Dipak Ram
BDC 2686

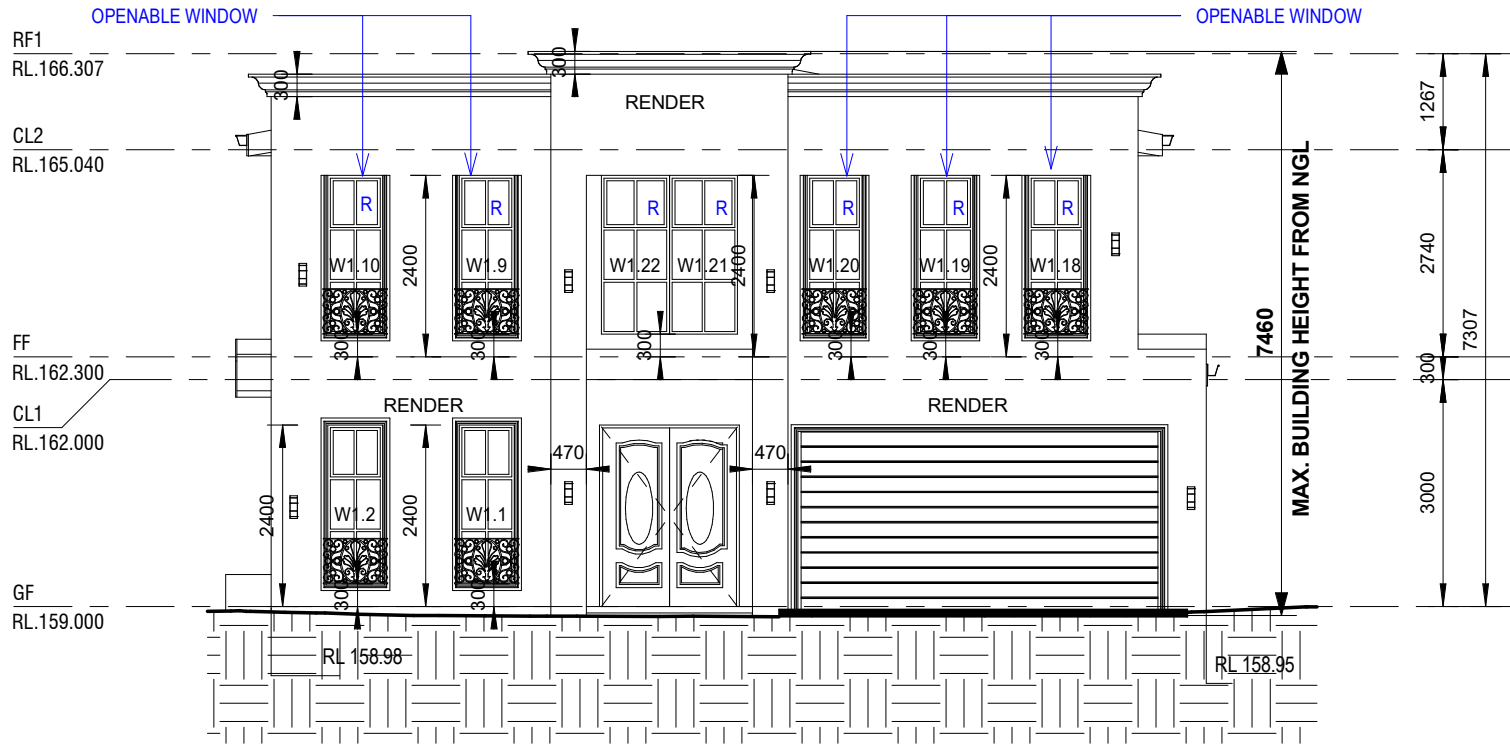

1 NORTH WEST ELEVATION
A03 1 : 100

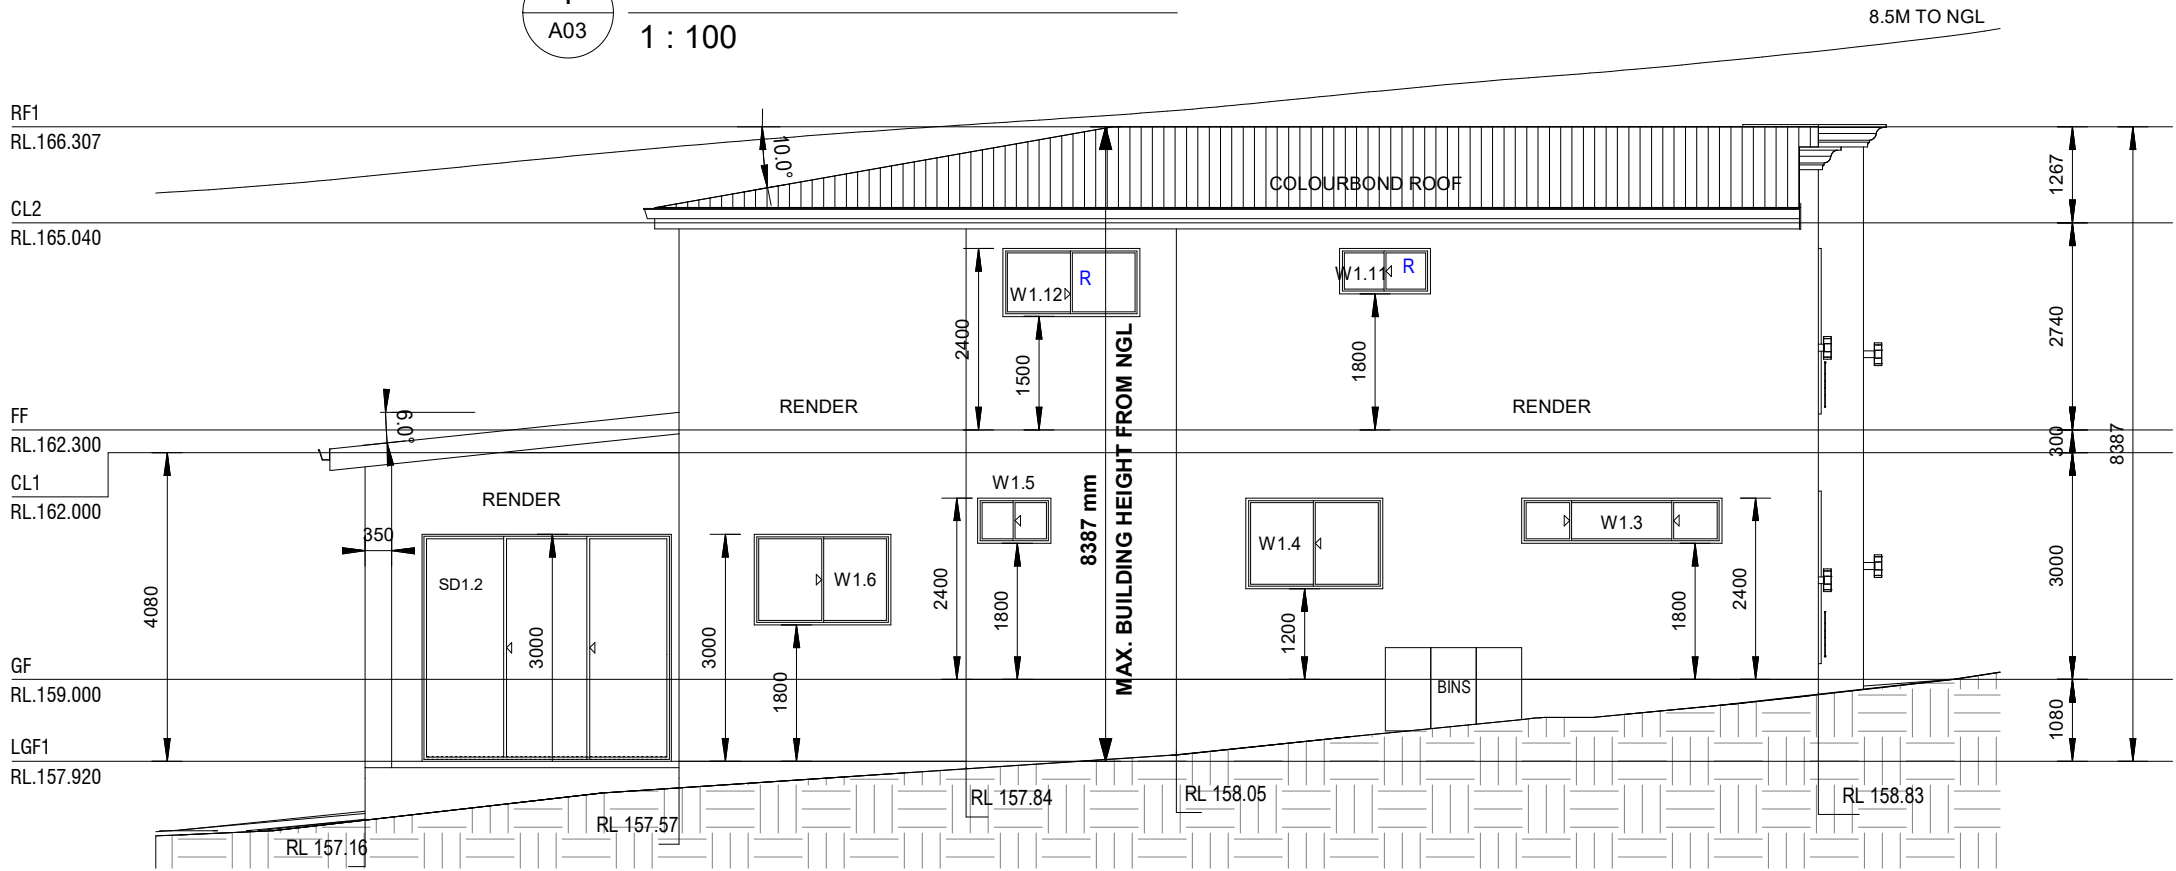

2 NORTH EAST ELEVATION
A03 1 : 100

NOTES:

1. ALL DIMENSIONS AND FLOOR AREAS TO BE VERIFIED PRIOR TO THE COMMENCEMENT OF ANY BUILDING WORK
2. ANY DISCREPANCIES ARE TO BE CONFIRMED BY THE DESIGNER
3. LEVELS SHOWN ARE APPROXIMATE UNLESS ACCOMPANIED BY REDUCED LEVELS BY A REGISTERED SURVEYOR
4. FIGURED DIMENSIONS ARE TO BE TAKEN IN PREFERENCE TO SCALING
5. ALL BOUNDARY CLEARANCE MUST BE VERIFIED BY THE SURVEYOR PRIOR TO THE COMMENCEMENT OF ANY BUILDING WORK
6. WHERE ENGINEERING OR HYDRAULIC DRAWINGS ARE REQUIRED, SUCH MUST TAKE PREFERENCE TO THIS DRAWING.
7. STORMWATER TO BE CONNECTED AND DISCHARGED TO COUNCIL'S REQUIREMENTS AND TO AS 3500.3
8. ALL SERVICES TO BE LOCATED AND VERIFIED BY THE BUILDER WITH THE RELEVANT AUTHORITIES PRIOR TO THE COMMENCEMENT OF ANY BUILDING.

ADDRESS:

**3 WINDSOR CT CASTLE HILL (LOT 1)
LOT 92 DP 786466**

CLIENT:

MR. REHAN FIROZ & MR.SALMAN FIROZ

B	REVISION	14-05-2026
A	ISSUED FOR CC	08-02-2026
ISSUE	REVISION	DATE

ISSUE:

B

TRUE NORTH:

CHECKED BY:

D.NOBEL

DRAWN BY:

A.PERVAIZ

DRAWING TITLE:

ELEVATIONS - PART 1

DRAWING NUMBER:

A03

SCALE:

As indicated @ A3




ABN: 51 463 906 127
UNIT 1/128-130 VICTORIA STREET WERRINGTON NSW 2747
0431231255, info@adadesign.com.au
NOMINATED ARCHITECT: DENIS NOBEL (REG.12432)

NOTE: WHERE FLOOR LEVEL IS >2M ABOVE EXTERNAL SURFACE BENEATH WINDOW, AND WHERE THE OPENABLE SASH IS <1.7M, ANY OPENABLE WINDOW IN A BEDROOM MUST BE RESTRICTED TO A 125MM OPENING.


IN REGARDS TO OTHER ROOMS, THIS APPLIES WHERE THE FLOOR LEVEL IS >4M. R DENOTES RESTRICTION ON THE WINDOW

Construction Certificate (CC)

Dipak Ram
BDC 2686

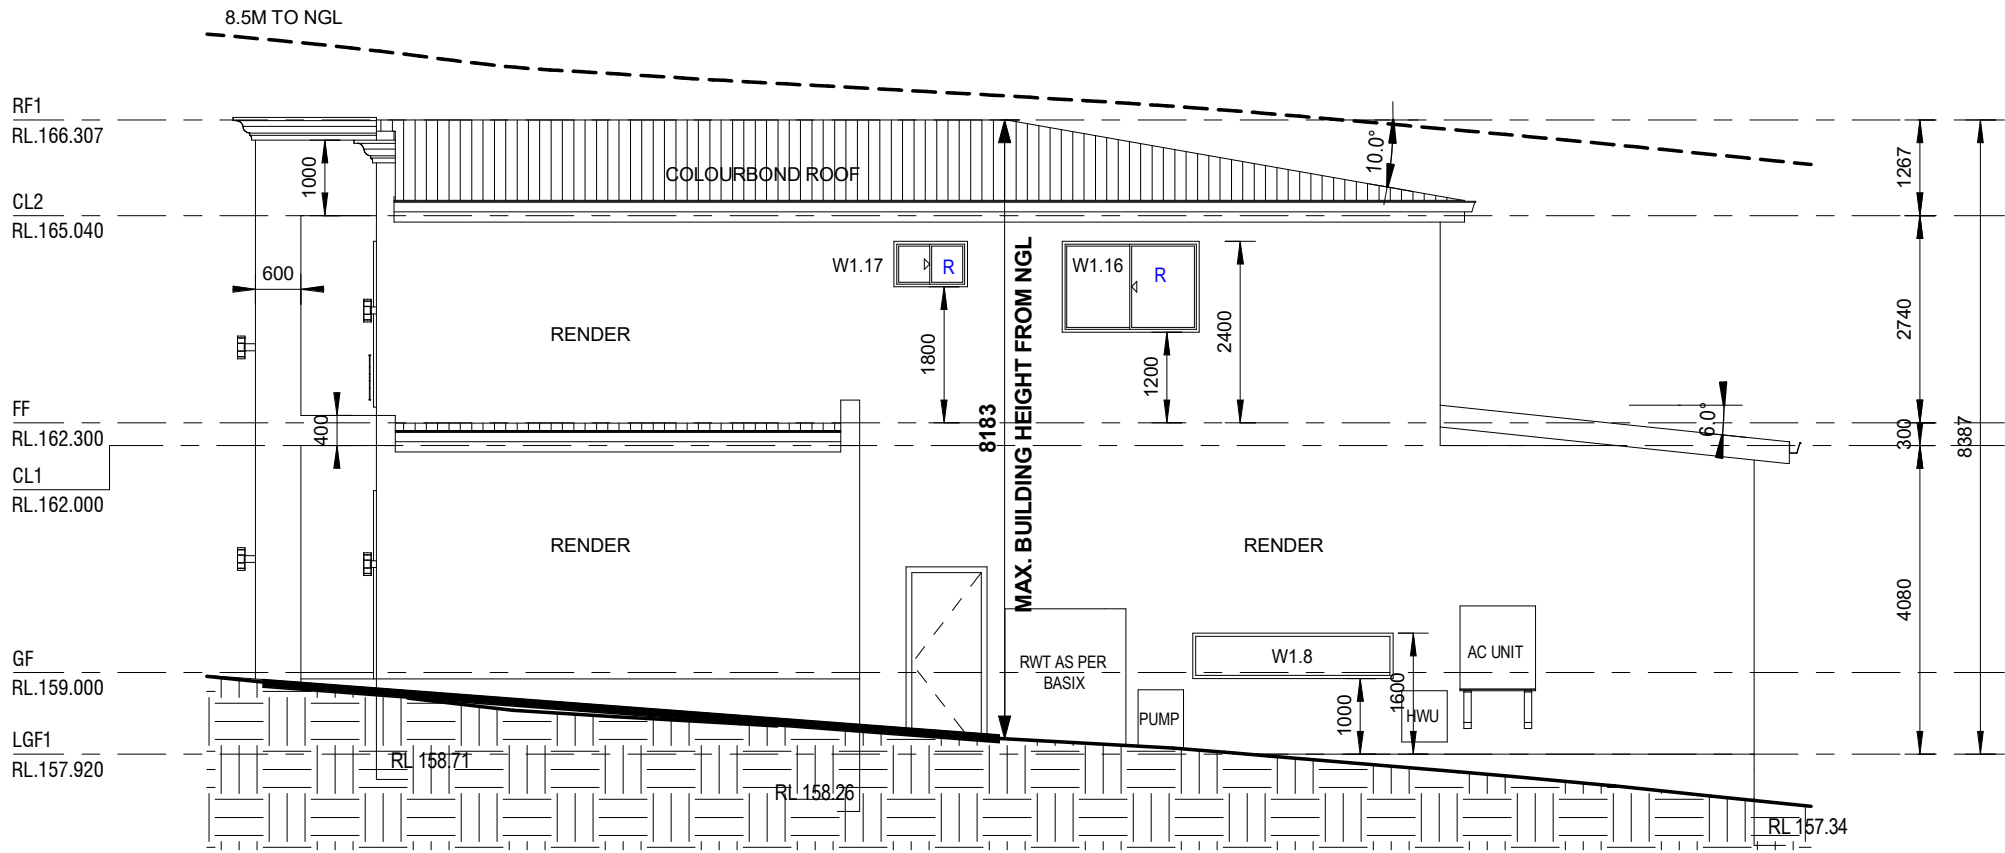

1 SOUTH WEST ELEVATION
A04 1 : 100

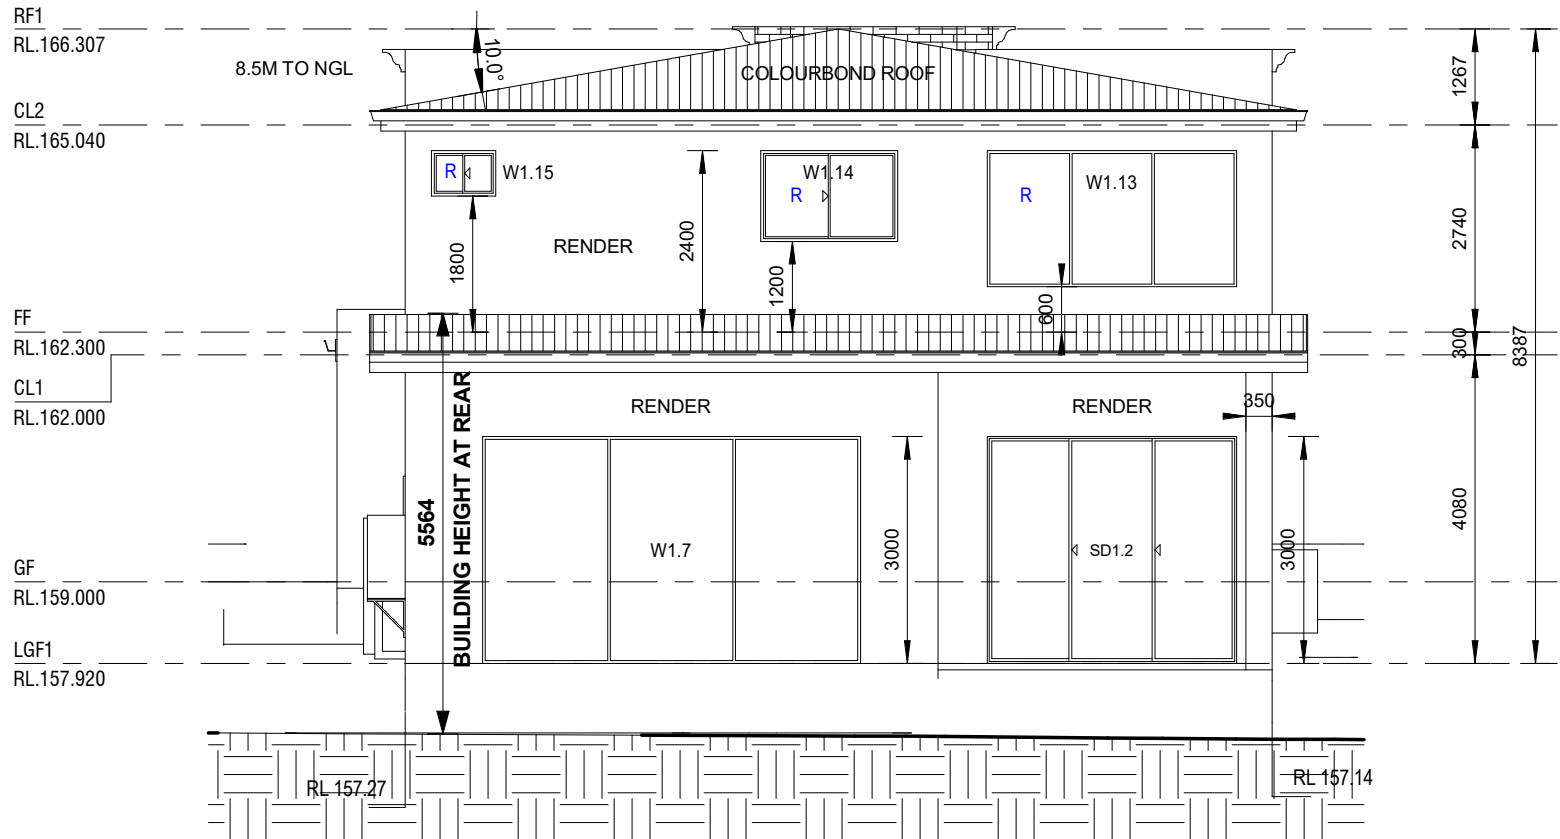

2 SOUTH EAST ELEVATION
A04 1 : 100

NOTES:

1. ALL DIMENSIONS AND FLOOR AREAS TO BE VERIFIED PRIOR TO THE COMMENCEMENT OF ANY BUILDING WORK
2. ANY DISCREPANCIES ARE TO BE CONFIRMED BY THE DESIGNER
3. LEVELS SHOWN ARE APPROXIMATE UNLESS ACCOMPANIED BY REDUCED LEVELS BY A REGISTERED SURVEYOR
4. FIGURED DIMENSIONS ARE TO BE TAKEN IN PREFERENCE TO SCALING
5. ALL BOUNDARY CLEARANCE MUST BE VERIFIED BY THE SURVEYOR PRIOR TO THE COMMENCEMENT OF ANY BUILDING WORK
6. WHERE ENGINEERING OR HYDRAULIC DRAWINGS ARE REQUIRED, SUCH MUST TAKE PREFERENCE TO THIS DRAWING
7. STORMWATER TO BE CONNECTED AND DISCHARGED TO COUNCIL'S REQUIREMENTS AND TO AS 3500.3
8. ALL SERVICES TO BE LOCATED AND VERIFIED BY THE BUILDER WITH THE RELEVANT AUTHORITIES PRIOR TO THE COMMENCEMENT OF ANY BUILDING

ADDRESS:

3 WINDSOR CT CASTLE HILL (LOT 1)
LOT 92 DP 786466

CLIENT:

MR. REHAN FIROZ & MR.SALMAN FIROZ

B	REVISION	14-05-2026
A	ISSUED FOR CC	08-02-2026
ISSUE	REVISION	DATE

ISSUE:

TRUE NORTH:

B

CHECKED BY: D.NOBEL

DRAWN BY: A.PERVAIZ

DRAWING TITLE:

ELEVATIONS PART-2

DRAWING NUMBER:

A04

SCALE:


As indicated @ A3



ABN: 51 463 906 127
UNIT 1/128-130 VICTORIA STREET WERRINGTON NSW 2747
0431231255, info@adadesign.com.au
NOMINATED ARCHITECT: DENIS NOBEL (REG.12432)

HOMECERTS PTY LTD
Reference: 26235/01
Date: 29/05/2026
Construction Certificate (CC)
Dipak Ram
BDC 2686



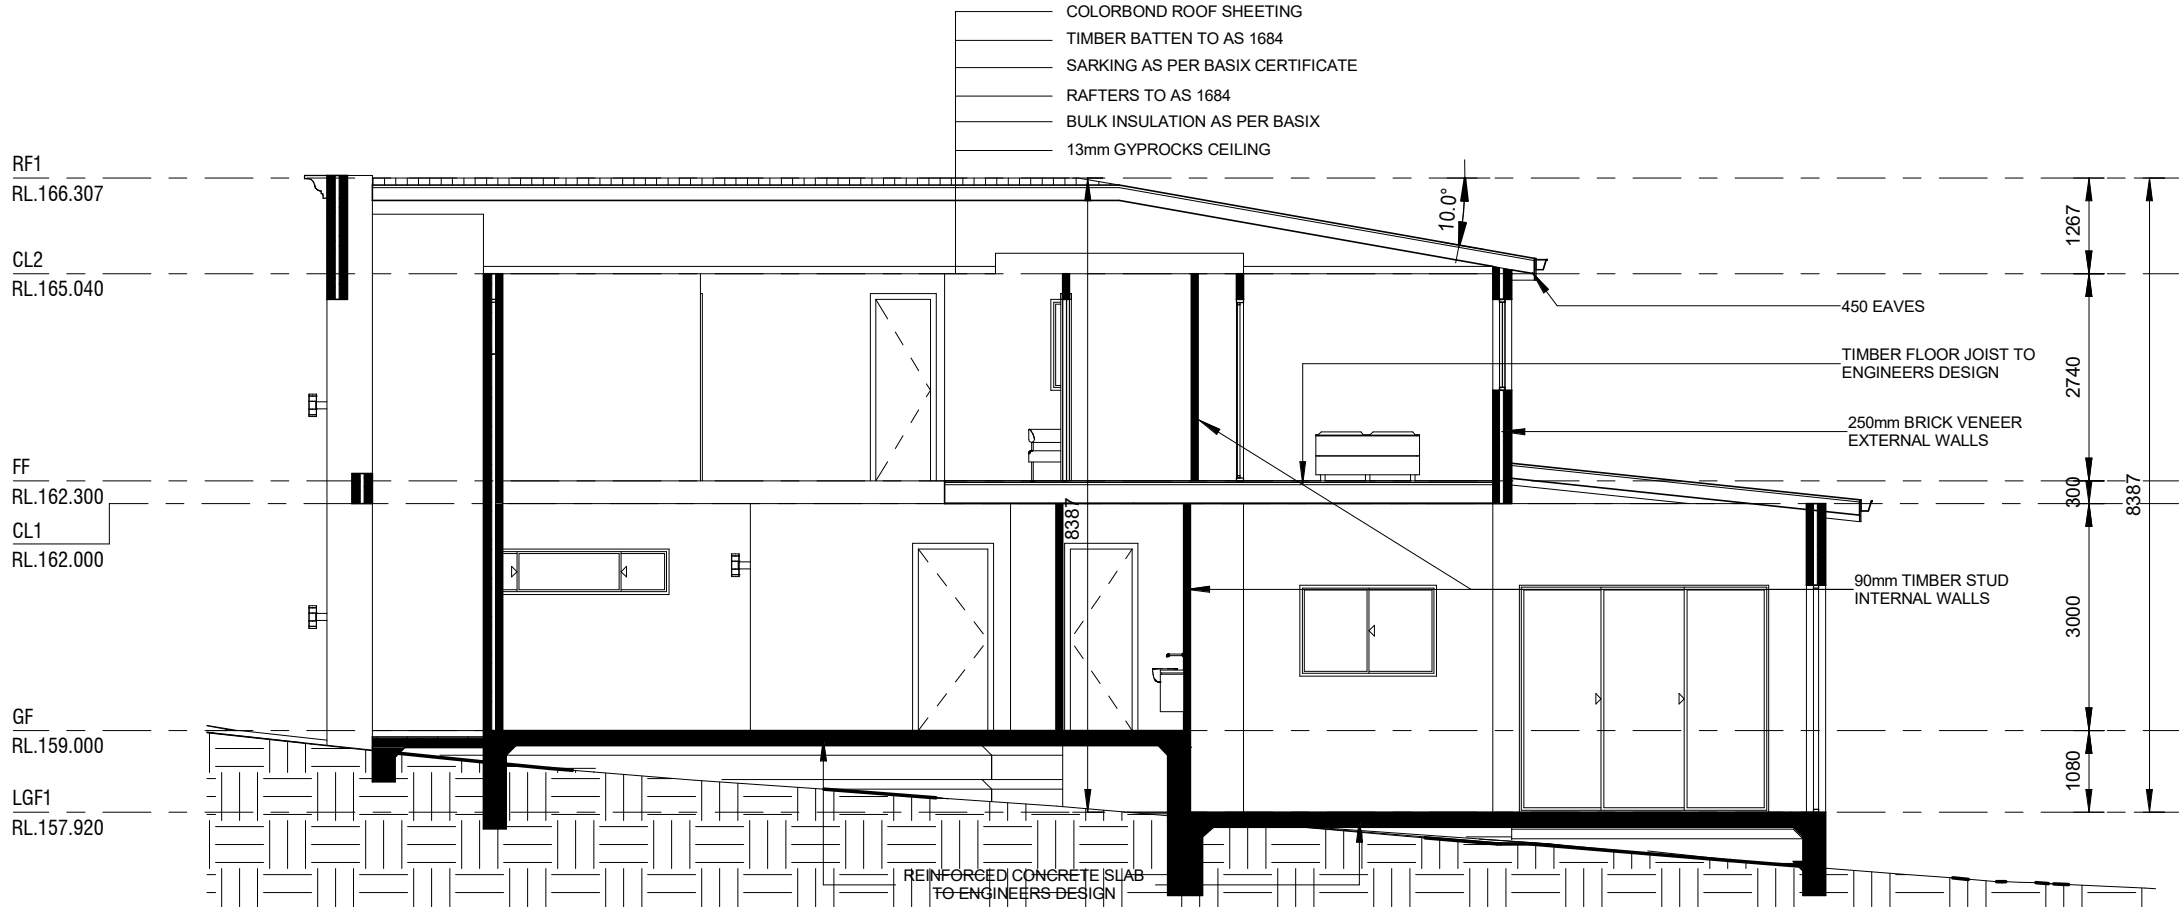


2

A05

SECTION - DW1

1 : 100

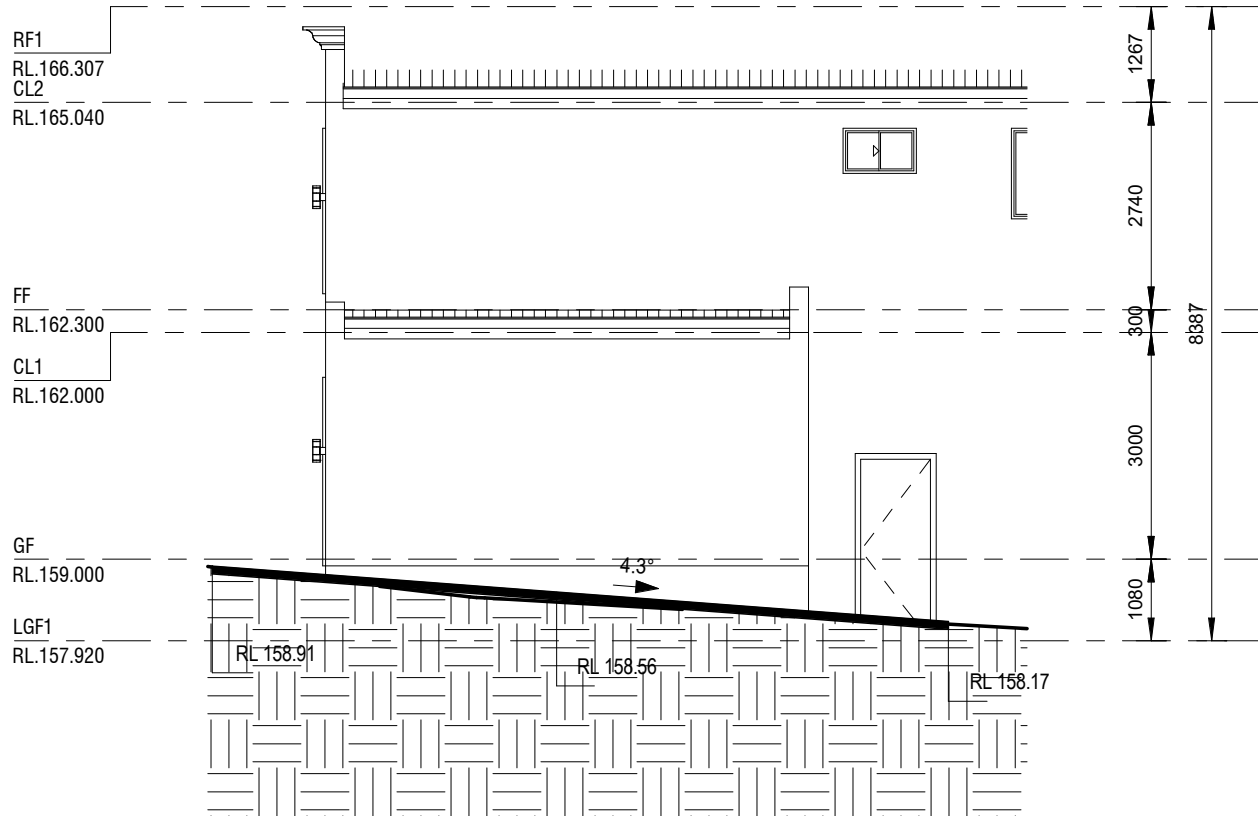

1

A05

SECTION - DW1 ENTRY TO LAUNDRY RAMP

1 : 100

NOTES:

- ALL DIMENSIONS AND FLOOR AREAS TO BE VERIFIED PRIOR TO THE COMMENCEMENT OF ANY BUILDING WORK
- ANY DISCREPANCIES ARE TO BE CONFIRMED BY THE DESIGNER
- LEVELS SHOWN ARE APPROXIMATE UNLESS ACCOMPANIED BY REDUCED LEVELS BY A REGISTERED SURVEYOR
- FIGURED DIMENSIONS ARE TO BE TAKEN IN PREFERENCE TO SCALING
- ALL BOUNDARY CLEARANCE MUST BE VERIFIED BY THE SURVEYOR PRIOR TO THE COMMENCEMENT OF ANY BUILDING WORK
- WHERE ENGINEERING OR HYDRAULIC DRAWINGS ARE REQUIRED, SUCH MUST TAKE PREFERENCE TO THIS DRAWING
- STORMWATER TO BE CONNECTED AND DISCHARGED TO COUNCIL'S REQUIREMENTS AND TO AS 3500.3
- ALL SERVICES TO BE LOCATED AND VERIFIED BY THE BUILDER WITH THE RELEVANT AUTHORITIES PRIOR TO THE COMMENCEMENT OF ANY BUILDING

ADDRESS:
3 WINDSOR CT CASTLE HILL (LOT 1)
LOT 92 DP 786466
CLIENT:
MR. REHAN FIROZ & MR.SALMAN FIROZ

B	REVISION	14-05-2026
A	ISSUED FOR CC	08-02-2026
ISSUE	REVISION	DATE

ISSUE: TRUE NORTH:
B
CHECKED BY: D.NOBEL
DRAWN BY: A.PERVAIZ

DRAWING TITLE:
SECTION PART-1
DRAWING NUMBER: A05
SCALE: 1 : 100 @ A3

ADA
design
ABN: 51 463 906 127
UNIT 1/128-130 VICTORIA STREET WERRINGTON NSW 2747
0431231255, info@adadesign.com.au
NOMINATED ARCHITECT: DENIS NOBEL (REG.12432)


HOMECERTS PTY LTD
Reference: 26235/01
Date: 29/05/2026
Construction Certificate (CC)
Dipak Ram
BDC 2686





1

SCHEDULE OF FINISHES

 

01: WHITE RENDER



02: MONUMENT RENDER



03: ALUMINIUM WINDOWS & DOORS



04: COLORBOND ROOF



05: FASCIA & GUTTER

NOTES:
1. ALL DIMENSIONS AND FLOOR AREAS TO BE VERIFIED PRIOR TO THE COMMENCEMENT OF ANY BUILDING WORK
2. ANY DISCREPANCIES ARE TO BE CONFIRMED BY THE DESIGNER
3. LEVELS SHOWN ARE APPROXIMATE UNLESS ACCOMPANIED BY REDUCED LEVELS BY A REGISTERED SURVEYOR
4. FIGURED DIMENSIONS ARE TO BE TAKEN IN PREFERENCE TO SCALING
5. ALL BOUNDARY CLEARANCE MUST BE VERIFIED BY THE SURVEYOR PRIOR TO THE COMMENCEMENT OF ANY BUILDING WORK
6. WHERE ENGINEERING OR HYDRAULIC DRAWINGS ARE REQUIRED, SUCH MUST TAKE PREFERENCE TO THIS DRAWING
7. STORMWATER TO BE CONNECTED AND DISCHARGED TO COUNCIL'S REQUIREMENTS AND TO AS 3500.3
8. ALL SERVICES TO BE LOCATED AND VERIFIED BY THE BUILDER WITH THE RELEVANT AUTHORITIES PRIOR TO THE COMMENCEMENT OF ANY BUILDING.

ADDRESS:
**3 WINDSOR CT CASTLE HILL (LOT 1)
LOT 92 DP 786466**

CLIENT:
MR. REHAN FIROZ & MR.SALMAN FIROZ

B	REVISION	14-05-2026
A	ISSUED FOR CC	08-02-2026
ISSUE	REVISION	DATE

ISSUE:
B

TRUE NORTH:

CHECKED BY: D.NOBEL
DRAWN BY: A.PERVAIZ

DRAWING TITLE:
SCHEDULE OF FINISHES

DRAWING NUMBER:
A10

SCALE:
@ A3



ABN: 51 463 906 127
UNIT 1/128-130 VICTORIA STREET WERRINGTON NSW 2747
0431231255, info@adadesign.com.au
NOMINATED ARCHITECT: DENIS NOBEL (REG.12432)

HOMECERTS PTY LTD
Reference: 26235/01
Date: 29/05/2026
Construction Certificate (CC)
Dipak Ram
BDC 2686



WINDOW SCHEDULE - DW1				
Mark	Height	Width	Area	Level
W1.1	2100	730	1.53 m²	GF
W1.2	2100	730	1.53 m²	GF
W1.3	600	2650	1.59 m²	GF
W1.4	1200	1810	2.17 m²	GF
W1.5	600	970	0.58 m²	GF
W1.6	1200	1810	2.17 m²	LGF1
W1.7	3000	5000	15.00 m²	LGF1
W1.8	600	2650	1.59 m²	LGF1
W1.9	2100	730	1.53 m²	FF
W1.10	2100	730	1.53 m²	FF
W1.11	600	1200	0.72 m²	FF
W1.12	900	1810	2.17 m²	FF
W1.13	1800	3300	5.94 m²	FF
W1.14	1200	1810	2.17 m²	FF
W1.15	600	850	0.51 m²	FF
W1.16	1200	1810	2.17 m²	FF
W1.17	600	970	0.58 m²	FF
W1.18	2100	730	1.53 m²	FF
W1.19	2100	730	1.53 m²	FF
W1.20	2100	730	1.53 m²	FF
W1.21	2100	900	1.89 m²	FF
W1.22	2100	900	1.89 m²	FF

Grand total: 2251.89 m²

SLIDING DOOR SCHEDULE - DW1				
Mark	Height	Width	Area	Level
SD1.1	3000	3300	9.90 m²	LGF1
SD1.2	3000	3300	9.90 m²	LGF1

Grand total: 219.80 m²

NOTES:

- ALL DIMENSIONS AND FLOOR AREAS TO BE VERIFIED PRIOR TO THE COMMENCEMENT OF ANY BUILDING WORK
- ANY DISCREPANCIES ARE TO BE CONFIRMED BY THE DESIGNER
- LEVELS SHOWN ARE APPROXIMATE UNLESS ACCOMPANIED BY REDUCED LEVELS BY A REGISTERED SURVEYOR
- FIGURED DIMENSIONS ARE TO BE TAKEN IN PREFERENCE TO SCALING
- ALL BOUNDARY CLEARANCE MUST BE VERIFIED BY THE SURVEYOR PRIOR TO THE COMMENCEMENT OF ANY BUILDING WORK.
- WHERE ENGINEERING OR HYDRAULIC DRAWINGS ARE REQUIRED , SUCH MUST TAKE PREFERENCE TO THIS DRAWING.
- STORMWATER TO BE CONNECTED AND DISCHARGED TO COUNCIL'S REQUIREMENTS AND TO AS 3500.3
- ALL SERVICES TO BE LOCATED AND VERIFIED BY THE BUILDER WITH THE RELEVANT AUTHORITIES PRIOR TO THE COMMENCEMENT OF ANY BUILDING.

ADDRESS:
3 WINDSOR CT CASTLE HILL (LOT 1)
LOT 92 DP 786466

CLIENT:
MR. REHAN FIROZ & MR.SALMAN FIROZ

B	REVISION	14-05-2026
A	ISSUED FOR CC	08-02-2026
ISSUE	REVISION	DATE

ISSUE: TRUE NORTH:

B

CHECKED BY: D.NOBEL

DRAWN BY: A.PERVAIZ

DRAWING TITLE:

WINDOWS & DOOR SCHEDULE

DRAWING NUMBER: A11

SCALE: @ A3



ABN: 51 463 906 127
UNIT 1/128-130 VICTORIA STREET WERRINGTON NSW 2747
0431231255, info@adadesign.com.au
NOMINATED ARCHITECT: DENIS NOBEL (REG.12432)