


HOMECERTS PTY LTD
Reference: 26234/01
Date: 29/05/2026
Construction Certificate (CC)
Dipak Ram
BDC 2686



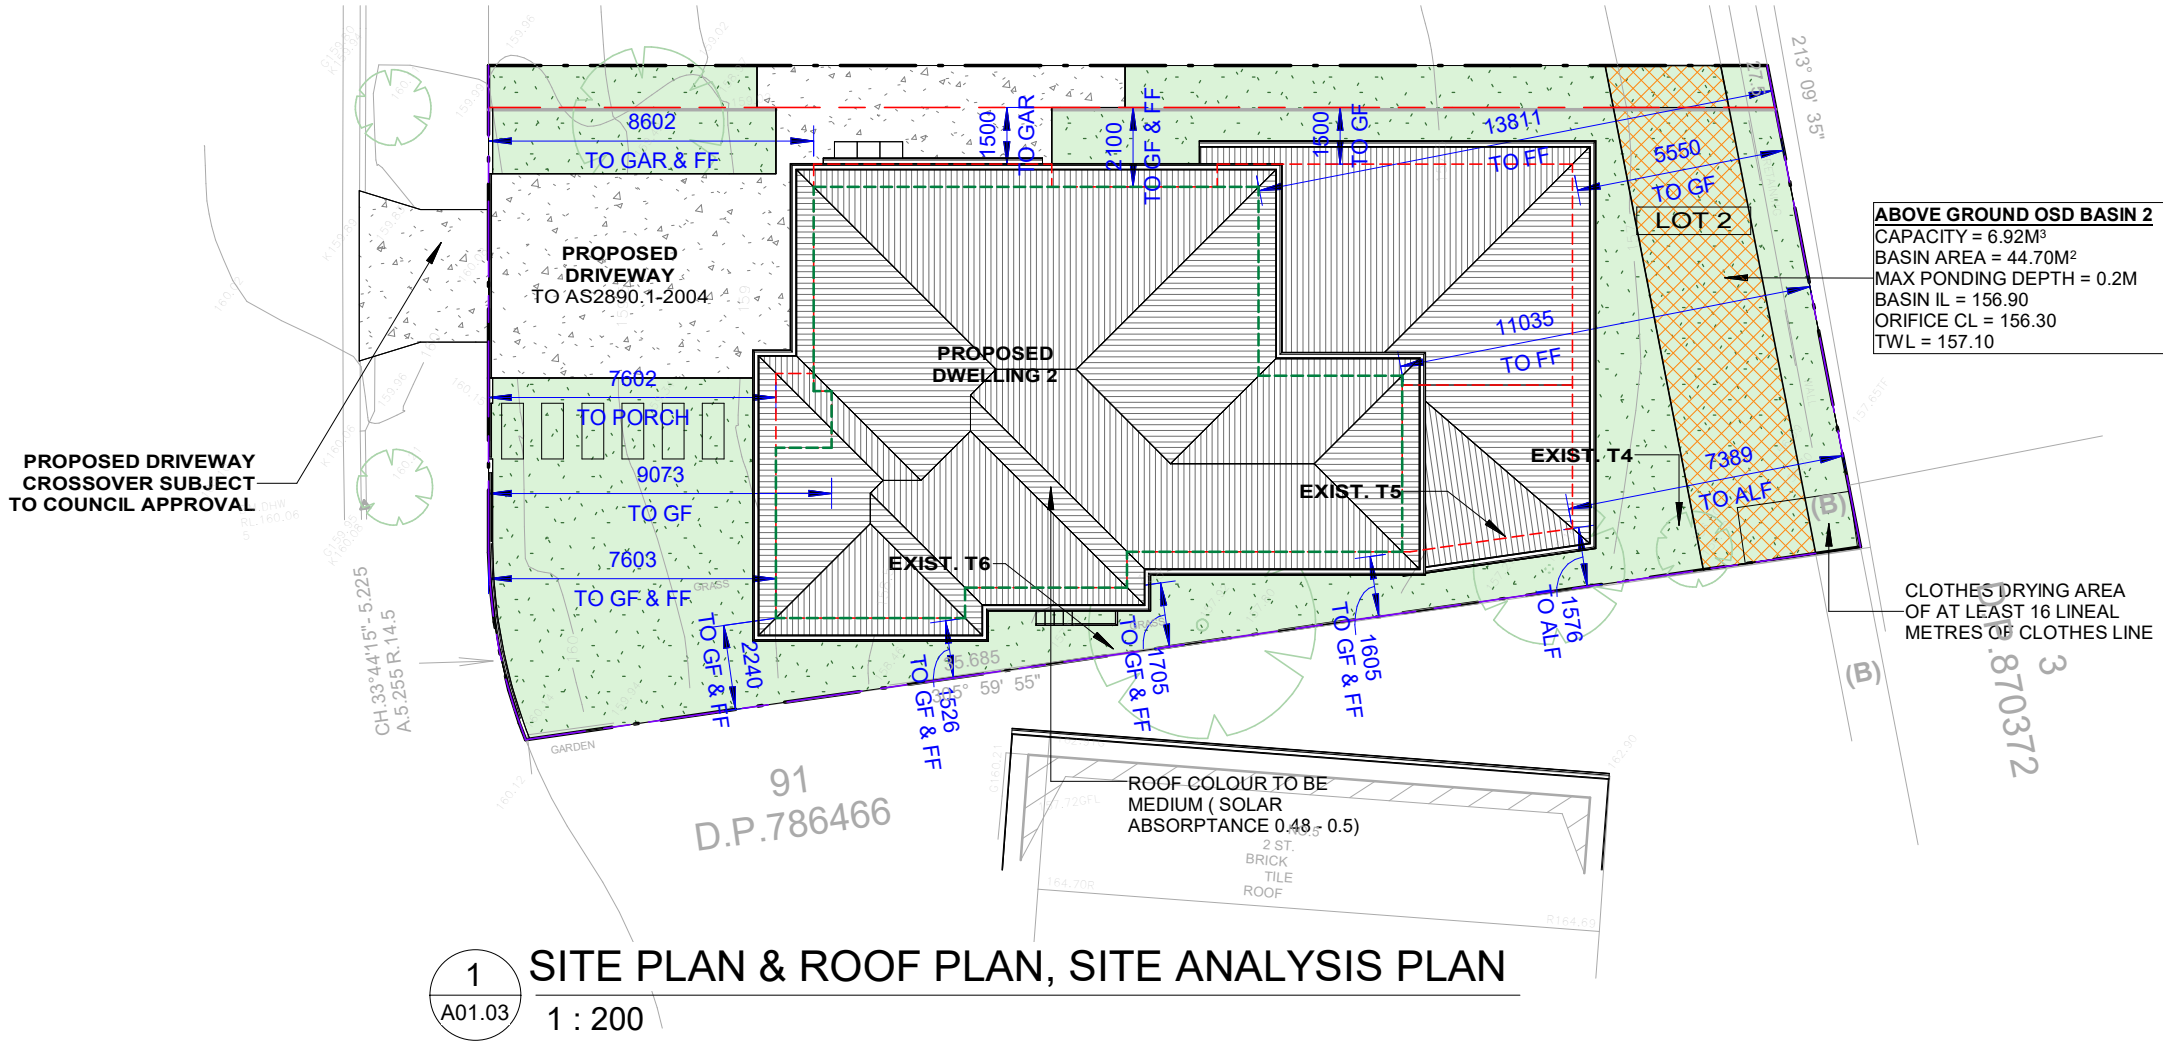

BASIX™ Certificate

Building Sustainability Index
www.planningportal.nsw.gov.au/development-and-assessment/basix

Single Dwelling

Certificate number: 1769657S_03

This certificate confirms that the proposed development will meet the NSW government's requirements for sustainability, if it is built in accordance with the commitments set out below. Terms used in this certificate, or in the commitments, have the meaning given by the document entitled "BASIX Definitions" dated 10/09/2020 published by the Department. This document is available at www.planningportal.nsw.gov.au/definitions

Secretary
Date of issue: Friday, 20 March 2026
To be valid, this certificate must be submitted with a development application or lodged with a complying development certificate application within 3 months of the date of issue.



When submitting this BASIX certificate with a development application or complying development certificate application, it must be accompanied by NatHERS certificate 2LXEPU659V.

Project summary		
Project name	3A Windsor Court, Castle Hill_03	
Street address	3A WINDSOR COURT CASTLE HILL 2154	
Local Government Area	Hills Shire Council	
Plan type and plan number	Deposited Plan 786466	
Lot no.	92	
Section no.	-	
Project type	dwelling house (detached)	
No. of bedrooms	5	
Project score		
Water	✔ 44	Target 40
Thermal Performance	✔ Pass	Target Pass
Energy	✔ 72	Target 72
Materials	✔ -48	Target n/a

CC Plans to comply with the recommendations from the arborist as mentioned in the Arborist Report prepared by Growing My Way Tree Consultants dated January 2025

LEGEND:

-  SITE BOUNDARY
-  PROPOSED GROUND FLOOR OUTLINE
-  PROPOSED FIRST FLOOR OUTLINE
-  EXISTING EASEMENT
-  AS PER ARBORIST REPORT
-  AS PER ARBORIST REPORT

NOTES:
1. ALL DIMENSIONS AND FLOOR AREAS TO BE VERIFIED PRIOR TO THE COMMENCEMENT OF ANY BUILDING WORK
2. ANY DISCREPANCIES ARE TO BE CONFIRMED BY THE DESIGNER
3. LEVELS SHOWN ARE APPROXIMATE UNLESS ACCOMPANIED BY REDUCED LEVELS BY A REGISTERED SURVEYOR
4. FIGURED DIMENSIONS ARE TO BE TAKEN IN PREFERENCE TO SCALING
5. ALL BOUNDARY CLEARANCE MUST BE VERIFIED BY THE SURVEYOR PRIOR TO THE COMMENCEMENT OF ANY BUILDING WORK
6. WHERE ENGINEERING OR HYDRAULIC DRAWINGS ARE REQUIRED, SUCH MUST TAKE PREFERENCE TO THIS DRAWING
7. STORMWATER TO BE CONNECTED AND DISCHARGED TO COUNCIL'S REQUIREMENTS AND TO AS 3500.3
8. ALL SERVICES TO BE LOCATED AND VERIFIED BY THE BUILDER WITH THE RELEVANT AUTHORITIES PRIOR TO THE COMMENCEMENT OF ANY BUILDING.

ADDRESS:
3A WINDSOR CT CASTLE HILL (LOT 2)
LOT 92 DP 786466
CLIENT:
MR. REHAN FIROZ & MR.SALMAN FIROZ

B	REVISION	14-05-2026
A	ISSUED FOR CC	08-02-2026
ISSUE	REVISION	DATE

ISSUE:
B
TRUE NORTH:

CHECKED BY: D.NOBEL
DRAWN BY: A.PERVAIZ

DRAWING TITLE:
SITE PLAN & ROOF PLAN, SITE ANALYSIS PLAN
DRAWING NUMBER: A01.03
SCALE: 1 : 200 @ A3

ADA design
ABN: 51 463 906 127
UNIT 1/128-130 VICTORIA STREET WERRINGTON NSW 2747
0431231255, info@adadesign.com.au
NOMINATED ARCHITECT: DENIS NOBEL (REG.12432)



LEGEND:

	SITE BOUNDARY
	PROPOSED DWELLING
	PROPOSED DRIVEWAY & CONCRETE AREAS
	PROPOSED LANDSCAPING
	MIN. POS 24m ²
	EXISTING EASEMENT
BS	PROPOSED SHRUB <i>Bursaria Spinosa (Blackthorn) 1m</i>
T1-2	PROPOSED TREE ACACIA BINERVIA (<i>Myall Wattle</i>) 5m SIZE: MIN. 75 LTR
T3-4	PROPOSED TREE ACACIA BINERVIA (<i>Myall Wattle</i>) 8m SIZE: MIN. 75 LTR

NOTES:
MIN 50% OF THE OVERALL NUMBER OF TREES & SHRUBS SHOULD BE NATIVE TO THIS REGION


[illegible]

Tree Size	Height	Spread	Min Soil Area	Min soil depth
Large trees	>12m	>8m	10 x 10m	1200mm
Medium trees	8-12m	4-8m	6 x 6m	1000mm
Small trees	5-8m	<4m	3.5 x 3.5m	800mm
Shrubs	-	-	n/a	500-600mm
Groundcover	-	-	n/a	300-450mm
Turf	-	-	n/a	200mm

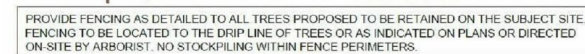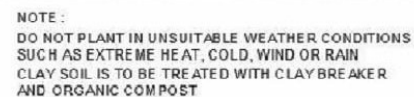

HOMECERTS PTY LTD
Reference: 26234/01
Date: 29/05/2026
Construction Certificate (CC)
Dipak Ram
BDC 2686



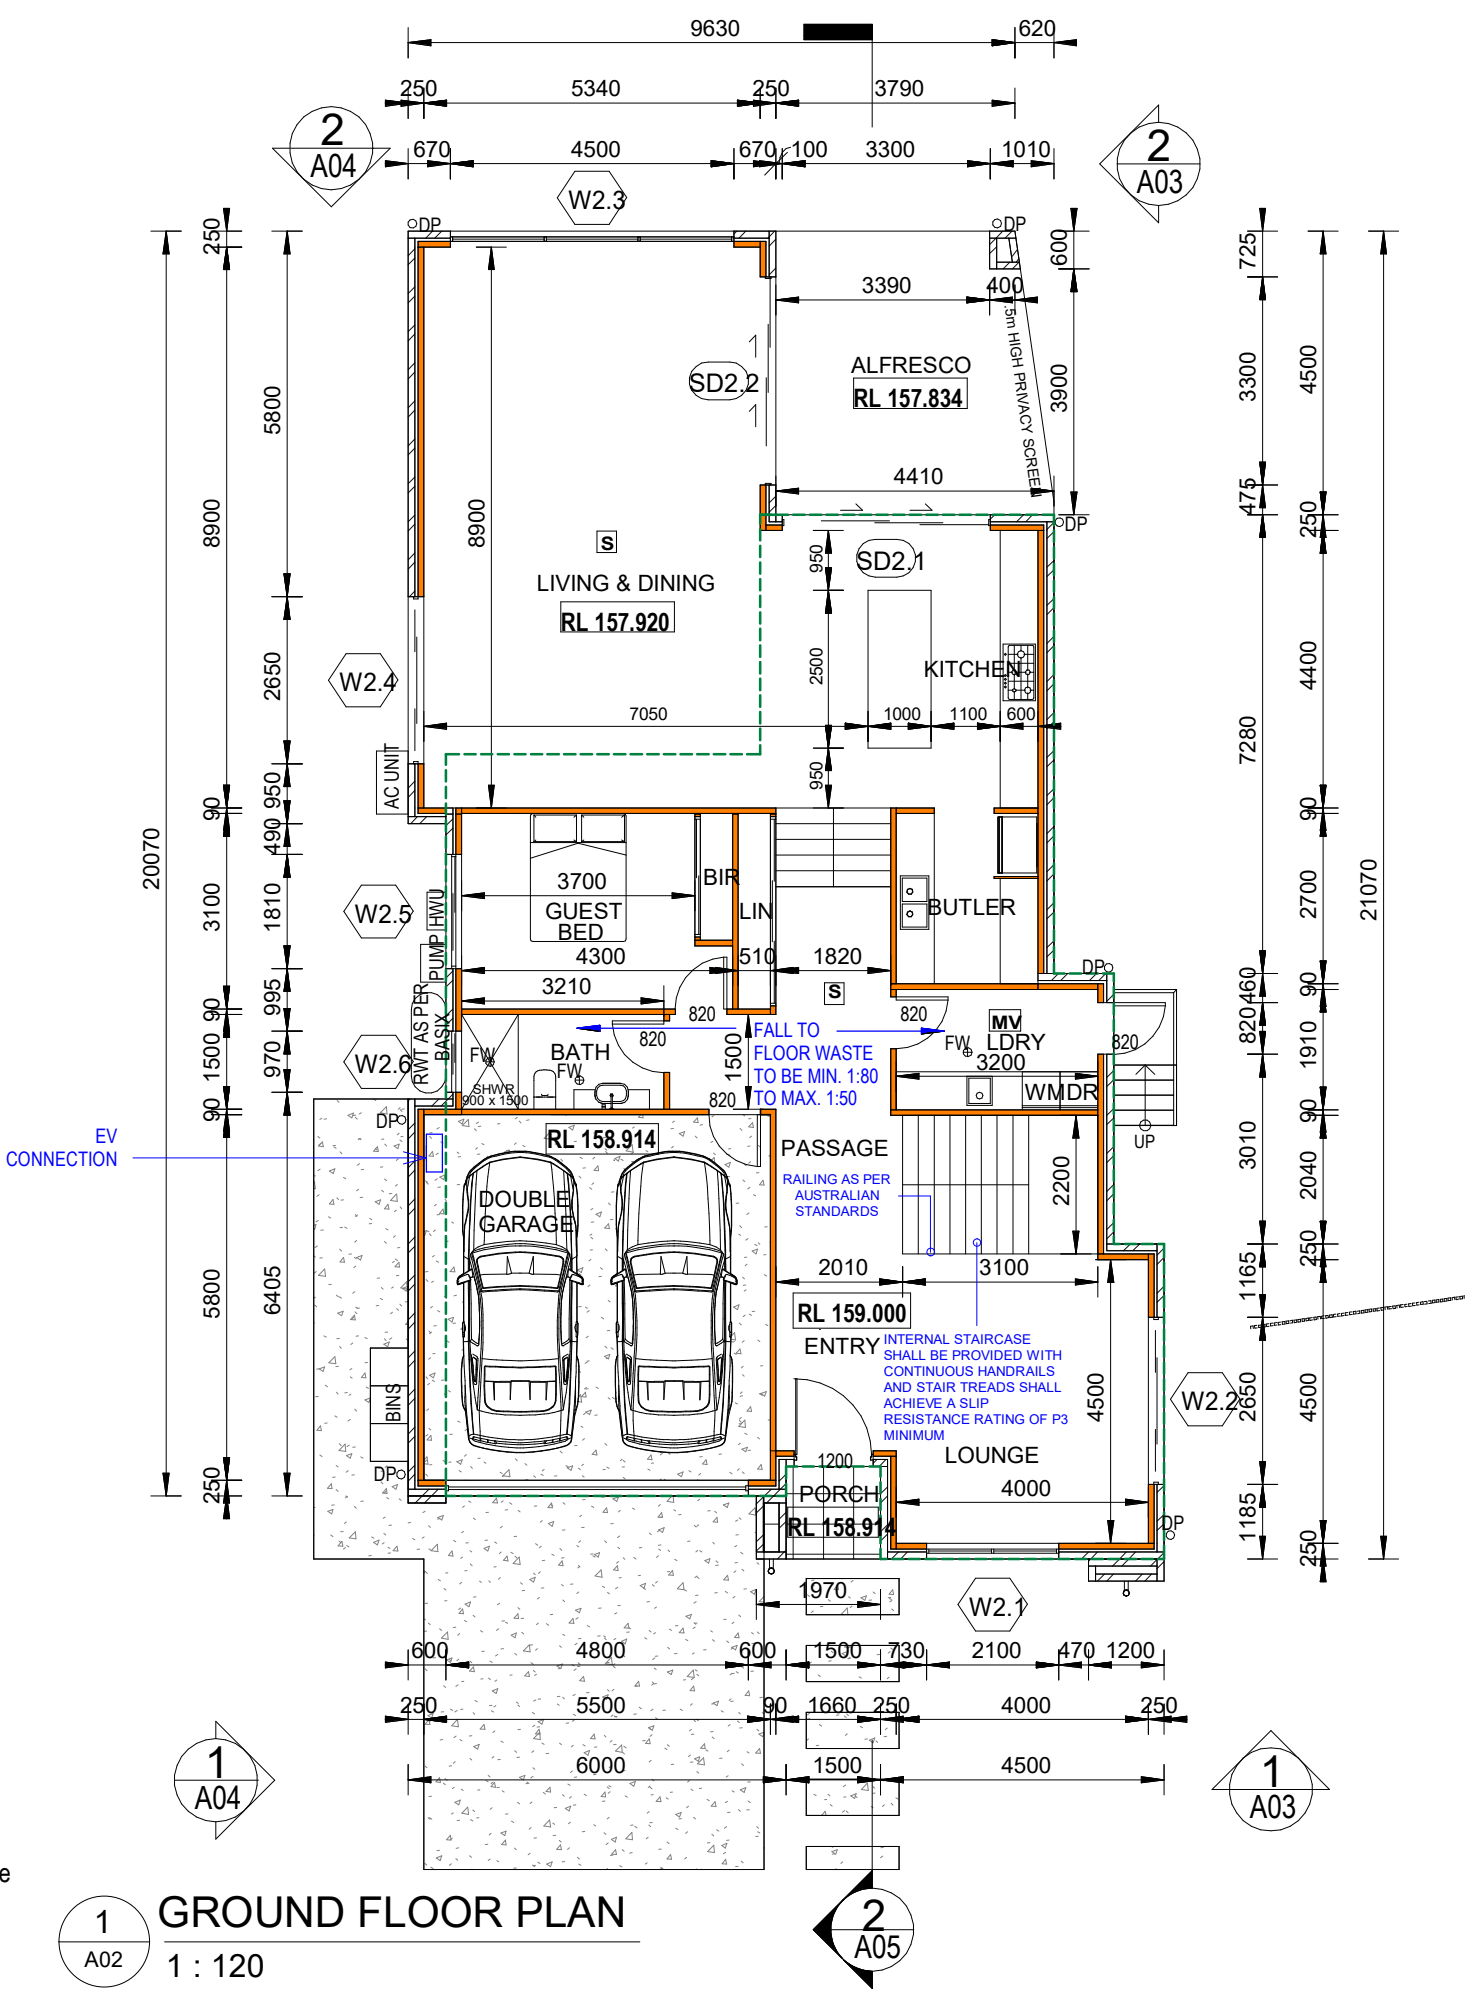

Note: Private EV connection of a minimum 15A circuit and power point to enable easy future EV connection in the garage connection to the main switch board.

1
A02

GROUND FLOOR PLAN

1 : 120

2
A05

NOTES:

- ALL DIMENSIONS AND FLOOR AREAS TO BE VERIFIED PRIOR TO THE COMMENCEMENT OF ANY BUILDING WORK
- ANY DISCREPANCIES ARE TO BE CONFIRMED BY THE DESIGNER
- LEVELS SHOWN ARE APPROXIMATE UNLESS ACCOMPANIED BY REDUCED LEVELS BY A REGISTERED SURVEYOR
- FIGURED DIMENSIONS ARE TO BE TAKEN IN PREFERENCE TO SCALING
- ALL BOUNDARY CLEARANCE MUST BE VERIFIED BY THE SURVEYOR PRIOR TO THE COMMENCEMENT OF ANY BUILDING WORK
- WHERE ENGINEERING OR HYDRAULIC DRAWINGS ARE REQUIRED, SUCH MUST TAKE PREFERENCE TO THIS DRAWING
- STORMWATER TO BE CONNECTED AND DISCHARGED TO COUNCIL'S REQUIREMENTS AND TO AS 3500.3
- ALL SERVICES TO BE LOCATED AND VERIFIED BY THE BUILDER WITH THE RELEVANT AUTHORITIES PRIOR TO THE COMMENCEMENT OF ANY BUILDING

ADDRESS:

**3A WINDSOR CT CASTLE HILL (LOT 2)
LOT 92 DP 786466**

CLIENT:

MR. REHAN FIROZ & MR.SALMAN FIROZ

B	REVISION	14-05-2026
A	ISSUED FOR CC	08-02-2026
ISSUE	REVISION	DATE

ISSUE:

B

CHECKED BY:

D.NOBEL

DRAWN BY:

A.PERVAIZ

TRUE NORTH:



DRAWING TITLE:

**PROPOSED DWELLING 2 GROUND
FLOOR PLAN**

DRAWING NUMBER:

A02

SCALE:

As indicated @ A3

NOTE: WHERE FLOOR LEVEL IS >2M ABOVE EXTERNAL SURFACE BENEATH WINDOW, AND WHERE THE OPENABLE SASH IS <1.7M, ANY OPENABLE WINDOW IN A BEDROOM MUST BE RESTRICTED TO A 125MM OPENING. IN REGARDS TO OTHER ROOMS, THIS APPLIES WHERE THE FLOOR LEVEL IS >4M. **R** DENOTES **R**ESTRICTION ON THE WINDOW

NOTE: **L/O** DENOTES **L**IFT **O**FF HINGES TO ALL WET AREAS

NOTE: REQUIRED ARTIFICIAL FLUORESCENT LIGHTING AS PER BASIX CERTIFICATE

NO DOWNLIGHTS TO BE INSTALLED ON FIRST FLOOR CEILING UNLESS SPECIFIED

NOTE: MECHANICAL VENTILATION TO BATHROOMS, ENSUITES, WC, LAUNDRIES MUST BE DUCTED TO OUTSIDE AIR

NOTE: WET AREA MUST COMPLY WITH ONE OF THE FOLLOWING: AS3740-2021 OR NCC PART 10.2

NOTE: **F** DENOTES FIXED WINDOW

NOTE: ALL WINDOWS & DOORS TO BE COMMERCIAL GRADE

NOTE: ROOF VENTILATION SHALL COMPLY WITH CLAUSE 10.8 OF THE NCC

NOTE: WET AREA SHALL BE WATERPROOFED AS PER CLAUSE 10.2 OF THE NCC- PUDDLE FLANGES SHALL BE FLUSHED WITH THE STRUCTURAL FLOOR AND ADEQUATELY WATERPROOFED.

NCC 2022 - ABCB HOUSING PROVISIONS 10.8.3 VENTILATION OF ROOF SPACES:

ROOF SPACE AS PER 10.8.3(1)(a) & (b) TO BE PROVIDED AND VENTILATION TO ROOF SPACE REQUIRED AS PER 10.8.3(1)(c).

EXHAUST FROM A BATHROOM, SANITARY COMPARTMENT TO DISCHARGE DIRECTLY TO OUTDOOR AIR. THIS EXHAUST SYSTEM MUST BE INTERLOCKED WITH LIGHT SWITCH AND INCLUDE RUN-ON TIMER SO THAT THE EXHAUST SYSTEM CONTINUES TO OPERATE FOR 10 MINUTES AFTER THE LIGHT SWITCH IS OFF.


GYPROCK SHAFT LINER PARTY WALL: DESIGN/CONSTRUCTION ARE TO COMPLY WITH BCA CLAUSE 9.3 FOR FIRE SEPARATION AND CLAUSE 10.7 FOR SOUND INSULATION. SEPARATING WALL TO ACHIEVE A MINIMUM FRL OF 60/60/60 AND SOUND INSULATION OF \$R_w + C_{tr}\$ (AIRBORNE) NOT LESS THAN 50 AND DISCONTINUOUS CONSTRUCTION. GYPROCK FIRE-RATED SEPARATING WALL-CENTRAL FIRE BARRIER COMPRISING—25 MM GYPROCK SHAFT LINER PANEL SECURED WITHIN GALVANISED STEEL CHANNELS AND HELD BY ALUMINIUM CLIPS DESIGNED FOR FIRE-AWAY RELEASE. MINIMUM 20 MM CAVITY ON BOTH SIDES OF THE SHAFT LINER PANEL. 70 MM OR 90 MM STEEL OR TIMBER STUDS SET BACK FROM THE LINER PANEL TO ENSURE DISCONTINUITY. 75 MM THICK GLASS WOOL INSULATION (MIN. DENSITY 11 KG/M³) OR EQUIVALENT POLYESTER INSULATION WITHIN THE STUD CAVITIES. 1 LAYER OF 13 MM GYPROCK PLASTERBOARD (E.G., SOUNDCEK OR FIRECEK) TO THE EXTERNAL FACE OF EACH STUD WALL.

ADA
design

ABN: 51 463 906 127
UNIT 1/128-130 VICTORIA STREET WERRINGTON NSW 2747
0431231255, info@adadesign.com.au
NOMINATED ARCHITECT: DENIS NOBEL (REG.12432)

HOMECERTS PTY LTD
Reference: 26234/01
Date: 29/05/2026
Construction Certificate (CC)
Dipak Ram
BDC 2686



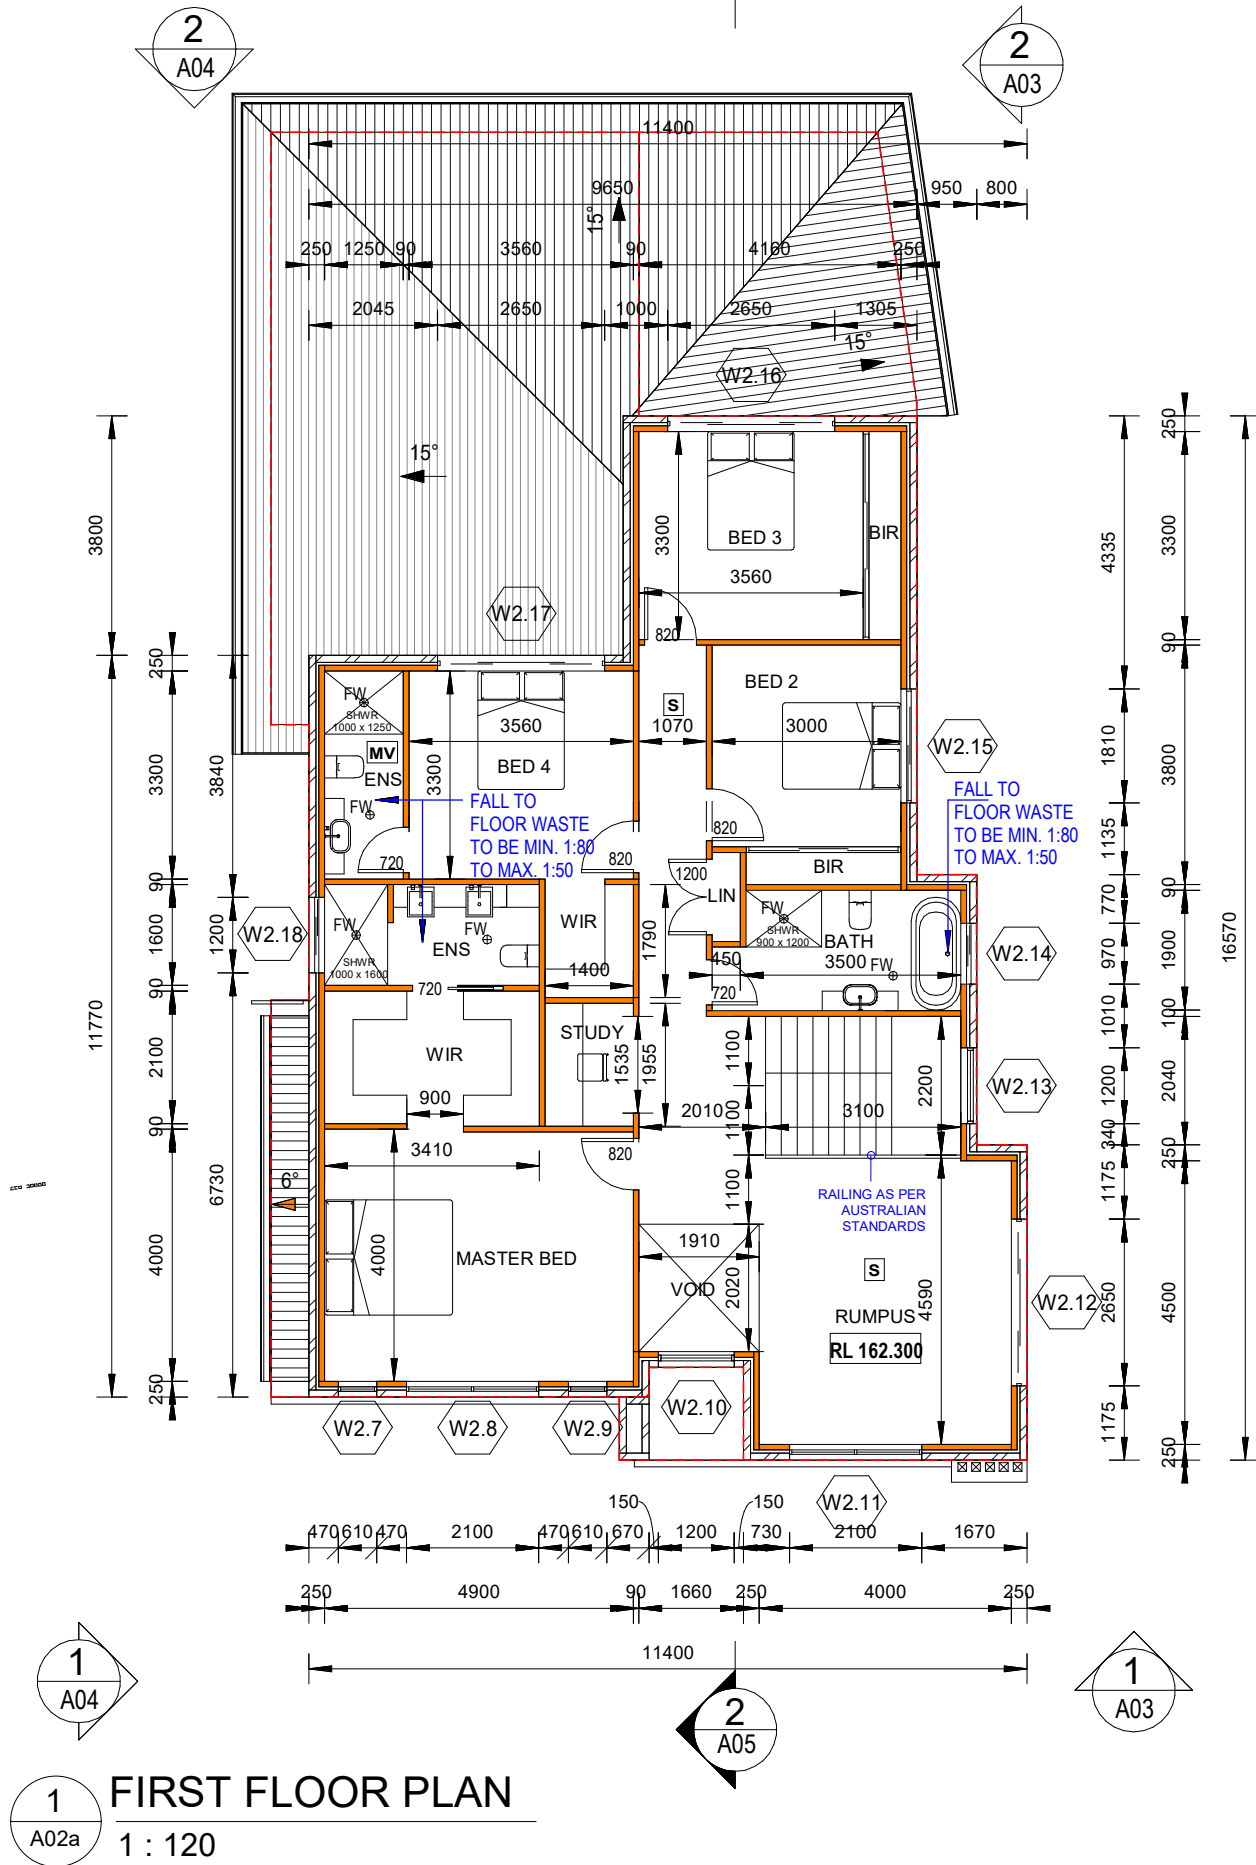

FLOOR AREA CALCULATIONS	
LOT 2 - DW2:	
PROPOSED GROUND FLOOR (INTERNAL):	149.0m ²
PROPOSED FIRST FLOOR (INTERNAL):	121.3m ²
PROPOSED GARAGE (INTERNAL) AREA:	31.9m ²
PROPOSED PORCH AREA:	2.3m ²
PROPOSED ALFRESCO AREA:	18.5m ²
TOTAL AREA:	323.0m²
TOTAL AREA (EXCLUDING PORCH AND ALFRESCO):	302.2m²

NOTE: WHERE FLOOR LEVEL IS >2M ABOVE EXTERNAL SURFACE BENEATH WINDOW, AND WHERE THE OPENABLE SASH IS <1.7M, ANY OPENABLE WINDOW IN A BEDROOM MUST BE RESTRICTED TO A 125MM OPENING. IN REGARDS TO OTHER ROOMS, THIS APPLIES WHERE THE FLOOR LEVEL IS >4M. **R** DENOTES **R**ESTRICTION ON THE WINDOW

NOTE: **L/O** DENOTES **L**IFT **O**FF HINGES TO ALL WET AREAS

NOTE: REQUIRED ARTIFICIAL FLUORESCENT LIGHTING AS PER BASIX CERTIFICATE

NO DOWNLIGHTS TO BE INSTALLED ON FIRST FLOOR CEILING UNLESS SPECIFIED

NOTE: MECHANICAL VENTILATION TO BATHROOMS, ENSUITES, WC, LAUNDRIES MUST BE DUCTED TO OUTSIDE AIR

NOTE: WET AREA MUST COMPLY WITH ONE OF THE FOLLOWING: AS3740-2021 OR NCC PART 10.2

NOTE: **E** DENOTES FIXED WINDOW

NOTE: ALL WINDOWS & DOORS TO BE COMMERCIAL GRADE

NOTE: ROOF VENTILATION SHALL COMPLY WITH CLAUSE 10.8 OF THE NCC

NOTE: WET AREA SHALL BE WATERPROOFED AS PER CLAUSE 10.2 OF THE NCC- PUDDLE FLANGES SHALL BE FLUSHED WITH THE STRUCTURAL FLOOR AND ADEQUATELY WATERPROOFED.

NCC 2022 - ABCB HOUSING PROVISIONS 10.8.3 VENTILATION OF ROOF SPACES:

ROOF SPACE AS PER 10.8.3(1)(a) & (b) TO BE PROVIDED AND VENTILATION TO ROOF SPACE REQUIRED AS PER 10.8.3(1)(c).

EXHAUST FROM A BATHROOM, SANITARY COMPARTMENT TO DISCHARGE DIRECTLY TO OUTDOOR AIR. THIS EXHAUST SYSTEM MUST BE INTERLOCKED WITH LIGHT SWITCH AND INCLUDE RUN-ON TIMER SO THAT THE EXHAUST SYSTEM CONTINUES TO OPERATE FOR 10 MINUTES AFTER THE LIGHT SWITCH IS OFF.

GYPROCK SHAFT LINER PARTY WALL: DESIGN/CONSTRUCTION ARE TO COMPLY WITH BCA CLAUSE 9.3 FOR FIRE SEPARATION AND CLAUSE 10.7 FOR SOUND INSULATION. SEPARATING WALL TO ACHIEVE A MINIMUM FRL OF 60/60/60 AND SOUND INSULATION OF $SR_w + C_{tr}$ (AIRBORNE) NOT LESS THAN 50 AND DISCONTINUOUS CONSTRUCTION. GYPROCK FIRE-RATED SEPARATING WALL: CENTRAL FIRE BARRIER COMPRISING—25 MM GYPROCK SHAFT LINER PANEL SECURED WITHIN GALVANISED STEEL CHANNELS AND HELD BY ALUMINIUM CLIPS DESIGNED FOR FIRE-AWAY RELEASE. MINIMUM 20 MM CAVITY ON BOTH SIDES OF THE SHAFT LINER PANEL. 70 MM OR 90 MM STEEL OR TIMBER STUDS SET BACK FROM THE LINER PANEL TO ENSURE DISCONTINUITY. 75 MM THICK GLASS WOOL INSULATION (MIN. DENSITY 11 KG/M³) OR EQUIVALENT POLYESTER INSULATION WITHIN THE STUD CAVITIES. 1 LAYER OF 13 MM GYPROCK PLASTERBOARD (E.G., SOUNDCEK OR FIRECEK) TO THE EXTERNAL FACE OF EACH STUD WALL.

- S** SMOKE ALARM SYSTEM
- MV** MECHANICAL VENTILATION
- FIRST FLOOR OUTLINE
- - - GROUND FLOOR OUTLINE

1 A04
1 A02a
FIRST FLOOR PLAN
1 : 120

NOTES:

- ALL DIMENSIONS AND FLOOR AREAS TO BE VERIFIED PRIOR TO THE COMMENCEMENT OF ANY BUILDING WORK
- ANY DISCREPANCIES ARE TO BE CONFIRMED BY THE DESIGNER
- LEVELS SHOWN ARE APPROXIMATE UNLESS ACCOMPANIED BY REDUCED LEVELS BY A REGISTERED SURVEYOR
- FIGURED DIMENSIONS ARE TO BE TAKEN IN PREFERENCE TO SCALING
- ALL BOUNDARY CLEARANCE MUST BE VERIFIED BY THE SURVEYOR PRIOR TO THE COMMENCEMENT OF ANY BUILDING WORK
- WHERE ENGINEERING OR HYDRAULIC DRAWINGS ARE REQUIRED, SUCH MUST TAKE PREFERENCE TO THIS DRAWING
- STORMWATER TO BE CONNECTED AND DISCHARGED TO COUNCIL'S REQUIREMENTS AND TO AS 3500.3
- ALL SERVICES TO BE LOCATED AND VERIFIED BY THE BUILDER WITH THE RELEVANT AUTHORITIES PRIOR TO THE COMMENCEMENT OF ANY BUILDING.

ADDRESS:
3A WINDSOR CT CASTLE HILL (LOT 2)
LOT 92 DP 786466

CLIENT:
MR. REHAN FIROZ & MR.SALMAN FIROZ

B	REVISION	14-05-2026
A	ISSUED FOR CC	08-02-2026
ISSUE	REVISION	DATE

ISSUE: **B**

TRUE NORTH: 

CHECKED BY: D.NOBEL

DRAWN BY: A.PERVAIZ

DRAWING TITLE:
PROPOSED DWELLING 2 FIRST FLOOR PLAN

DRAWING NUMBER: **A02a**

SCALE: **As indicated @ A3**

ADA
design


ABN: 51 463 906 127
UNIT 1/128-130 VICTORIA STREET WERRINGTON NSW 2747
0431231255, info@adadesign.com.au
NOMINATED ARCHITECT: DENIS NOBEL (REG.12432)

NOTE: WHERE FLOOR LEVEL IS >2M ABOVE EXTERNAL SURFACE BENEATH WINDOW, AND WHERE THE OPENABLE SASH IS <1.7M, ANY OPENABLE WINDOW IN A BEDROOM MUST BE RESTRICTED TO A 125MM OPENING.


IN REGARDS TO OTHER ROOMS, THIS APPLIES WHERE THE FLOOR LEVEL IS >4M. R DENOTES RESTRICTION ON THE WINDOW

Construction Certificate (CC)

Dipak Ram
BDC 2686

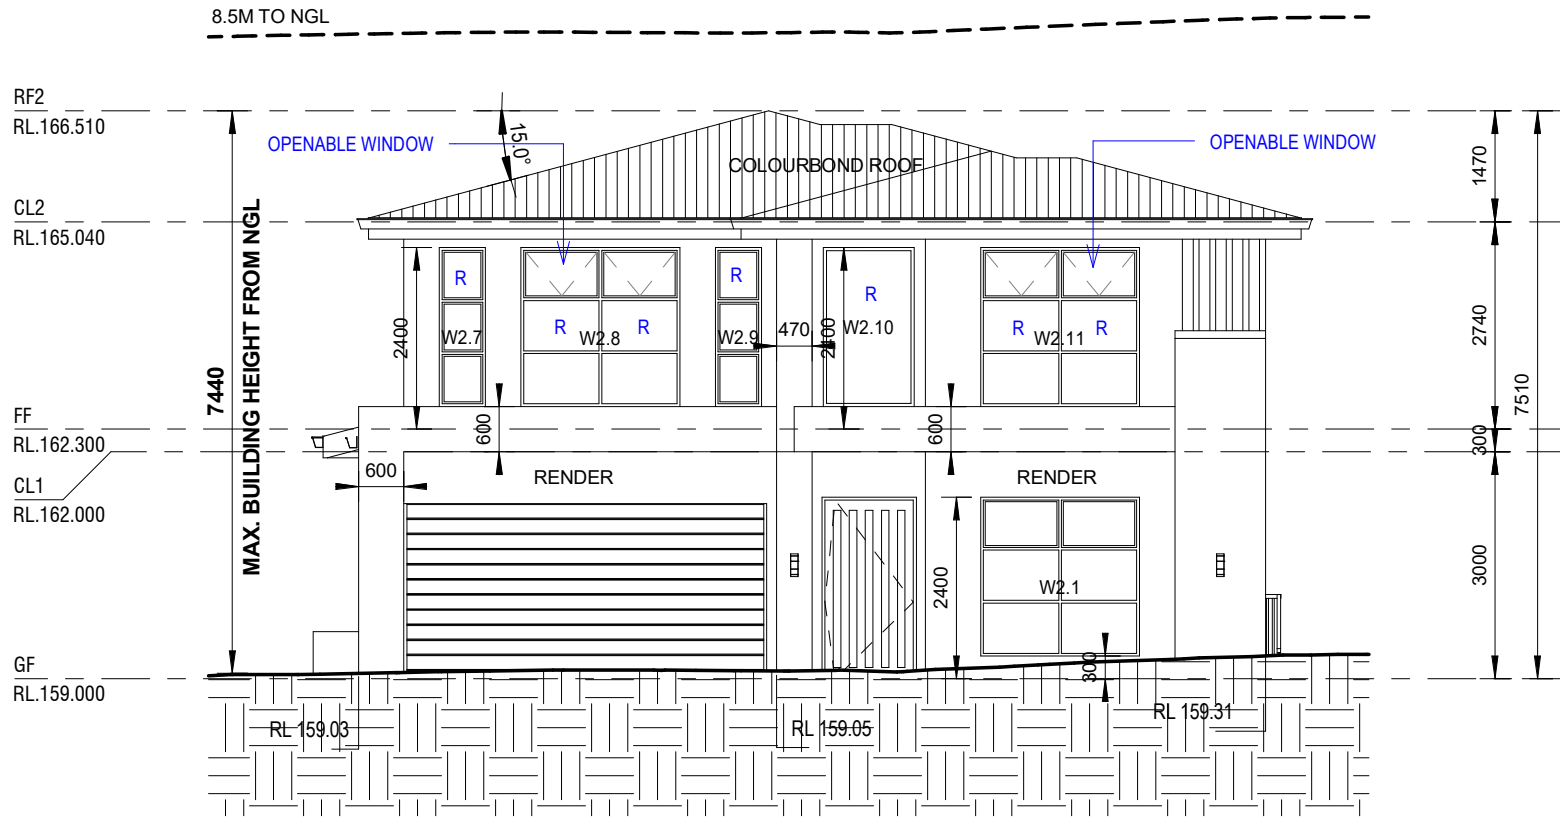

1 NORTH WEST ELEVATION
A03 1 : 100

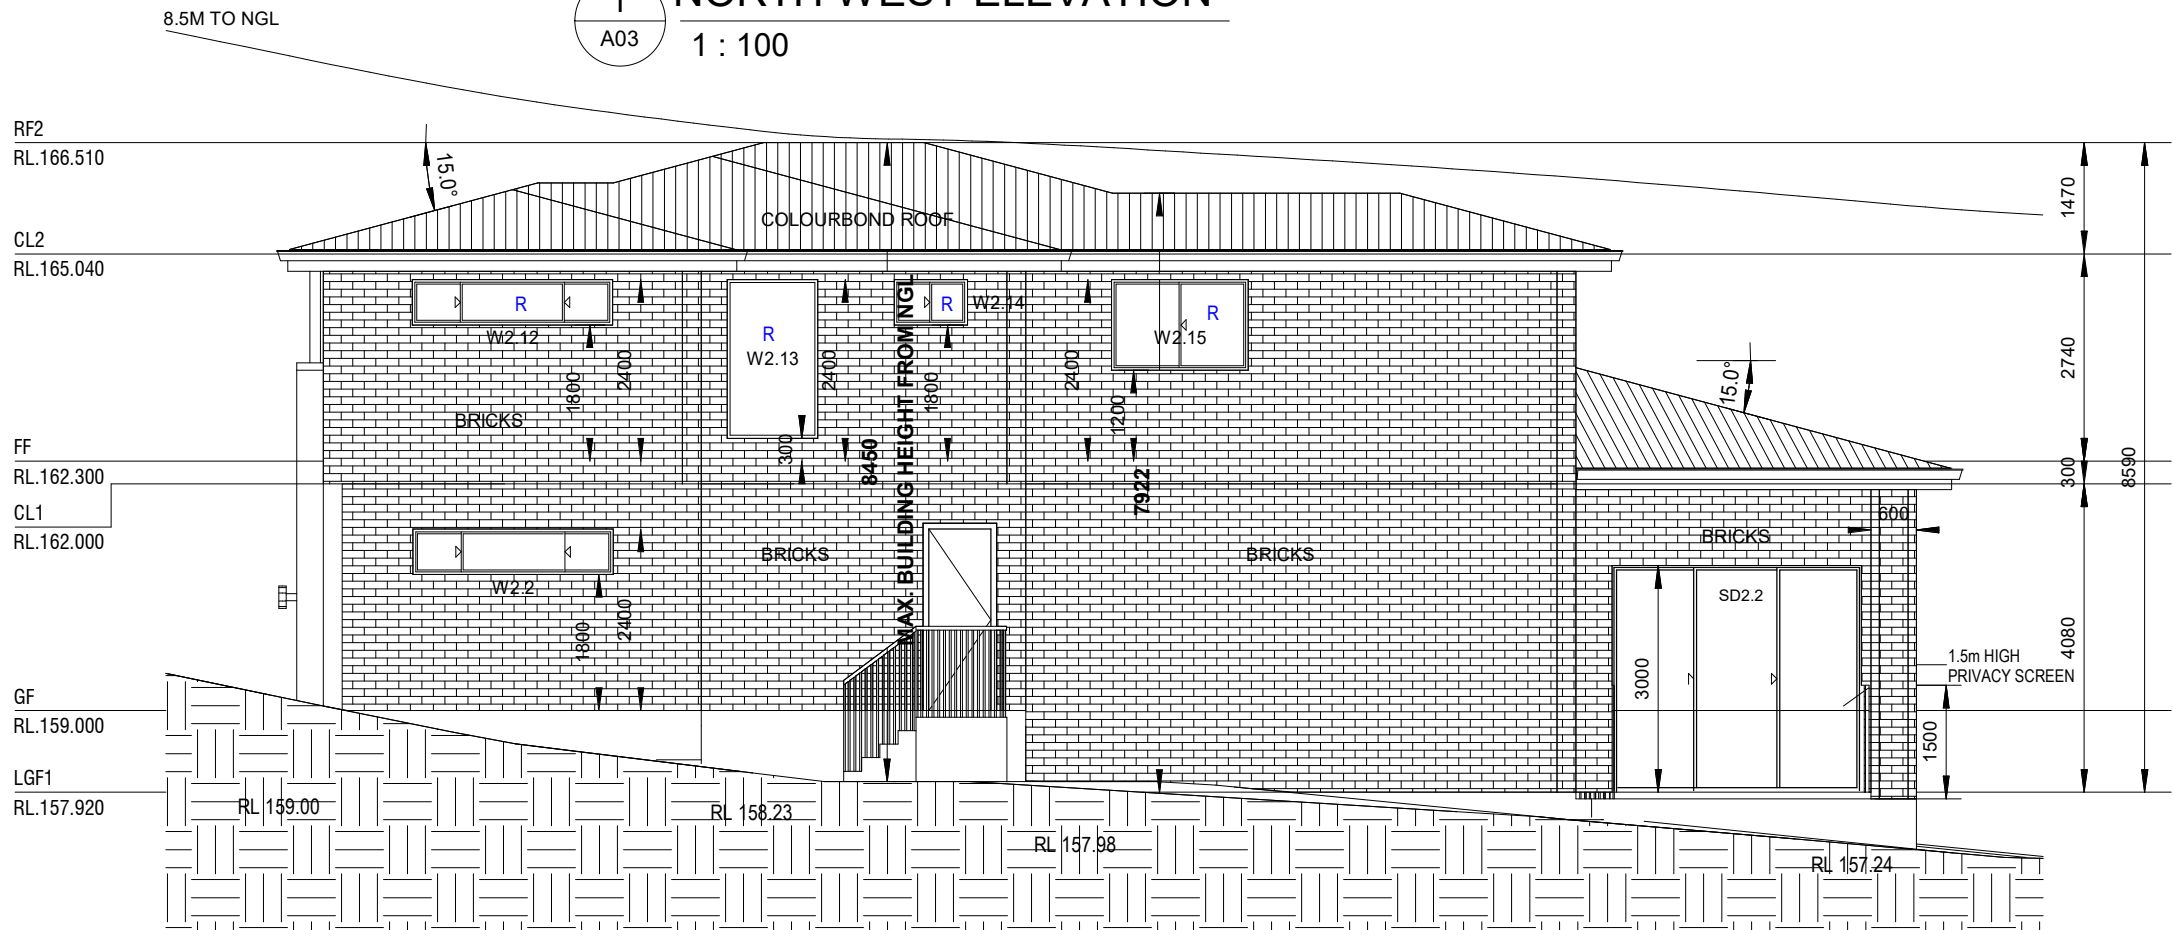

2 SOUTH WEST ELEVATION - DW2
A03 1 : 100

NOTES:

1. ALL DIMENSIONS AND FLOOR AREAS TO BE VERIFIED PRIOR TO THE COMMENCEMENT OF ANY BUILDING WORK
2. ANY DISCREPANCIES ARE TO BE CONFIRMED BY THE DESIGNER
3. LEVELS SHOWN ARE APPROXIMATE UNLESS ACCOMPANIED BY REDUCED LEVELS BY A REGISTERED SURVEYOR
4. FIGURED DIMENSIONS ARE TO BE TAKEN IN PREFERENCE TO SCALING
5. ALL BOUNDARY CLEARANCE MUST BE VERIFIED BY THE SURVEYOR PRIOR TO THE COMMENCEMENT OF ANY BUILDING WORK
6. WHERE ENGINEERING OR HYDRAULIC DRAWINGS ARE REQUIRED, SUCH MUST TAKE PREFERENCE TO THIS DRAWING
7. STORMWATER TO BE CONNECTED AND DISCHARGED TO COUNCIL'S REQUIREMENTS AND TO AS 3500.3
8. ALL SERVICES TO BE LOCATED AND VERIFIED BY THE BUILDER WITH THE RELEVANT AUTHORITIES PRIOR TO THE COMMENCEMENT OF ANY BUILDING

ADDRESS:

**3A WINDSOR CT CASTLE HILL (LOT 2)
LOT 92 DP 786466**

CLIENT:

MR. REHAN FIROZ & MR.SALMAN FIROZ

B	REVISION	14-05-2026
A	ISSUED FOR CC	08-02-2026
ISSUE	REVISION	DATE

ISSUE:

TRUE NORTH:

B

CHECKED BY: D.NOBEL

DRAWN BY: A.PERVAIZ

DRAWING TITLE:

ELEVATIONS - PART 1

DRAWING NUMBER:

A03

SCALE:


As indicated @ A3




ABN: 51 463 906 127
UNIT 1/128-130 VICTORIA STREET WERRINGTON NSW 2747
0431231255, info@adadesign.com.au
NOMINATED ARCHITECT: DENIS NOBEL (REG.12432)

NOTE: WHERE FLOOR LEVEL IS >2M ABOVE EXTERNAL SURFACE BENEATH WINDOW, AND WHERE THE OPENABLE SASH IS <1.7M, ANY OPENABLE WINDOW IN A BEDROOM MUST BE RESTRICTED TO A 125MM OPENING.
IN REGARDS TO OTHER ROOMS, THIS APPLIES WHERE THE FLOOR LEVEL IS >4M.
R DENOTES RESTRICTION ON THE WINDOW

Construction Certificate (CC)
Dipak Ram
BDC 2686

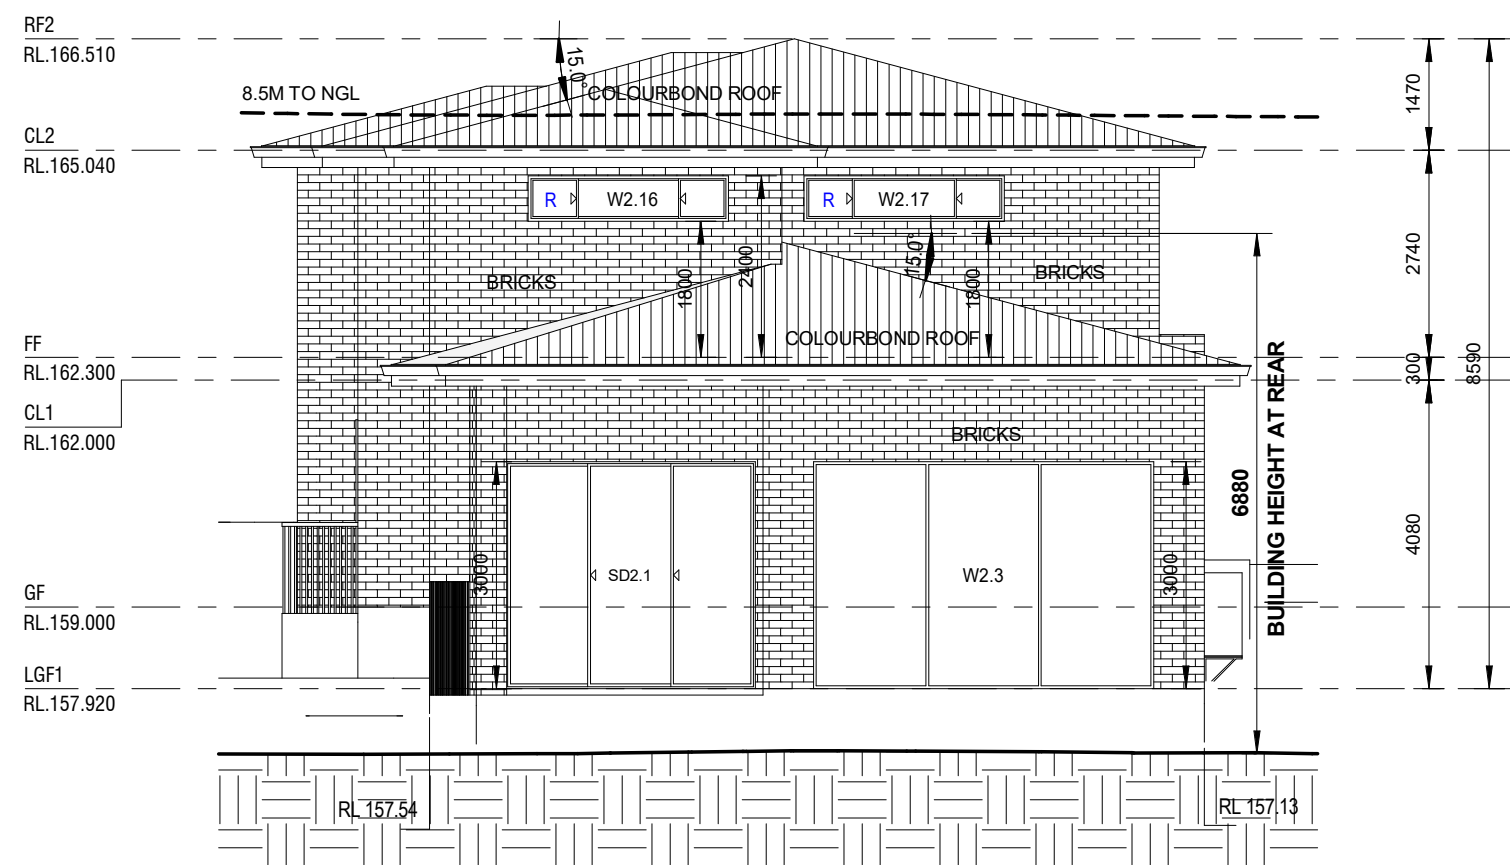

1 SOUTH EAST ELEVATION
A04 1 : 100

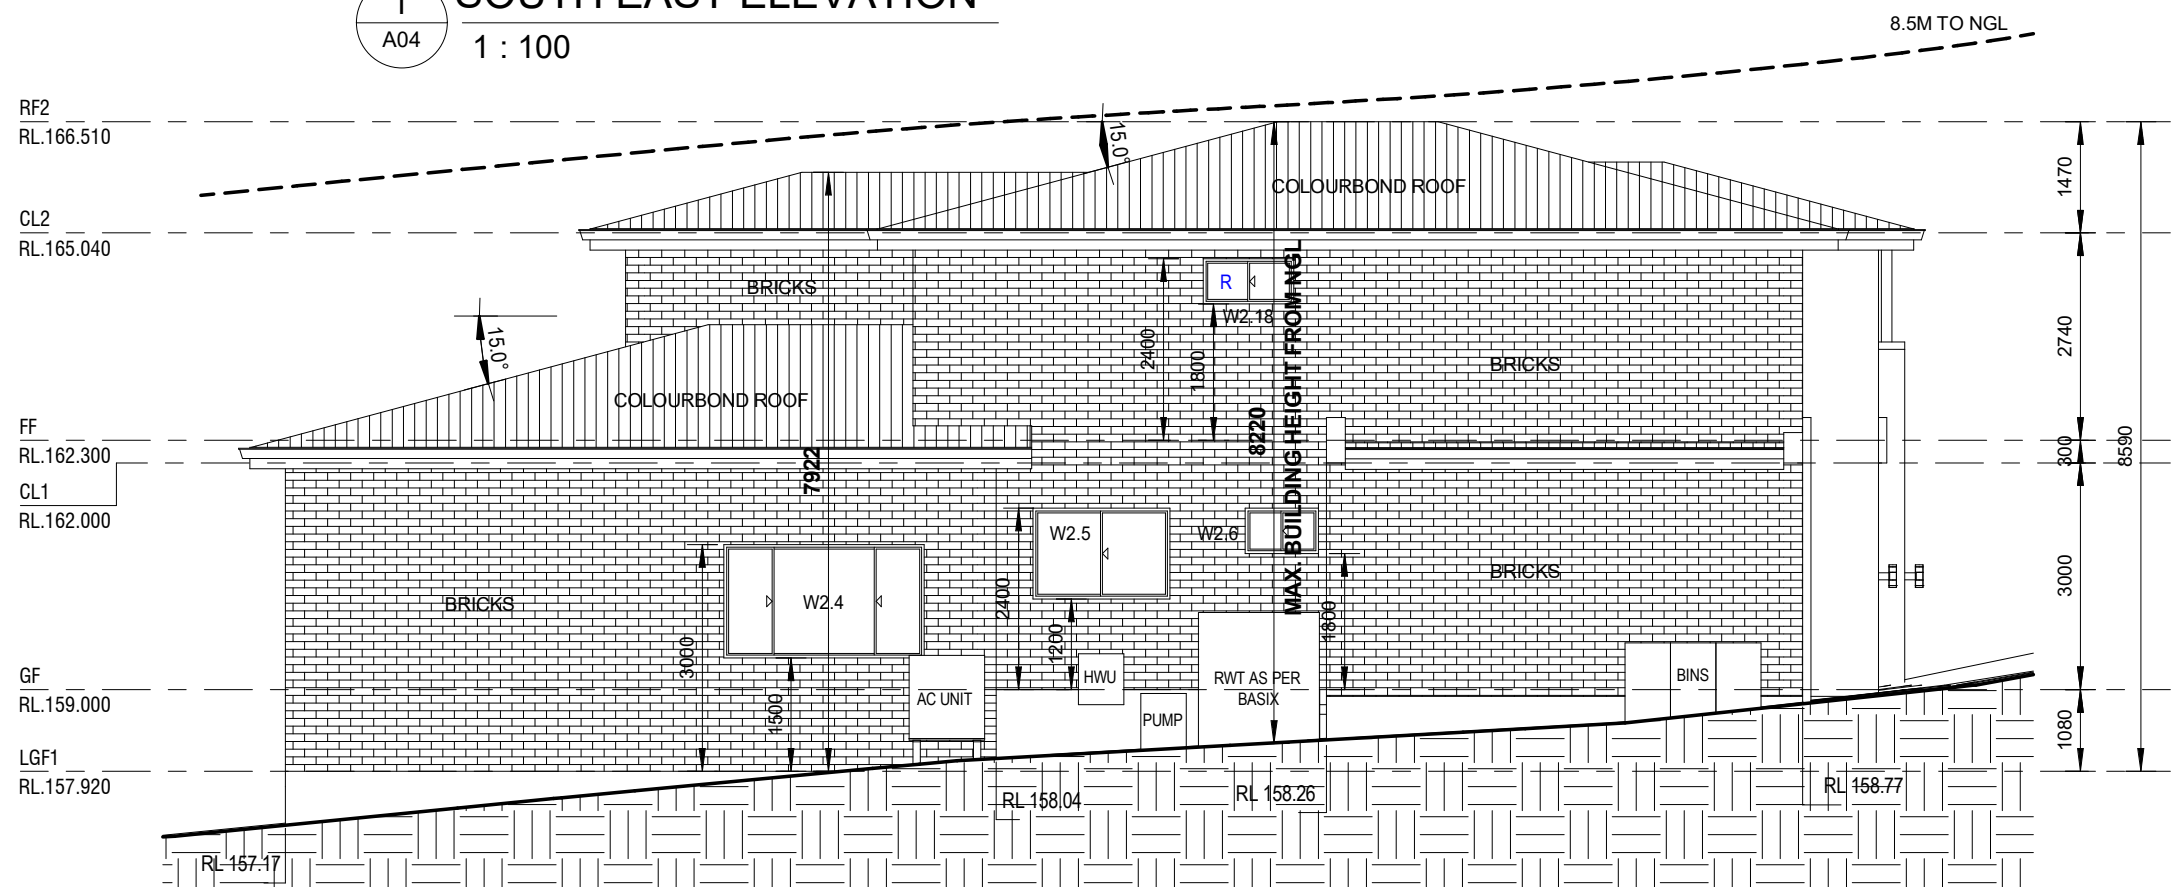

2 NORTH EAST ELEVATION - DW2
A04 1 : 100

NOTES:
1. ALL DIMENSIONS AND FLOOR AREAS TO BE VERIFIED PRIOR TO THE COMMENCEMENT OF ANY BUILDING WORK
2. ANY DISCREPANCIES ARE TO BE CONFIRMED BY THE DESIGNER
3. LEVELS SHOWN ARE APPROXIMATE UNLESS ACCOMPANIED BY REDUCED LEVELS BY A REGISTERED SURVEYOR
4. FIGURED DIMENSIONS ARE TO BE TAKEN IN PREFERENCE TO SCALING
5. ALL BOUNDARY CLEARANCE MUST BE VERIFIED BY THE SURVEYOR PRIOR TO THE COMMENCEMENT OF ANY BUILDING WORK
6. WHERE ENGINEERING OR HYDRAULIC DRAWINGS ARE REQUIRED, SUCH MUST TAKE PREFERENCE TO THIS DRAWING
7. STORMWATER TO BE CONNECTED AND DISCHARGED TO COUNCIL'S REQUIREMENTS AND TO AS 3500.3
8. ALL SERVICES TO BE LOCATED AND VERIFIED BY THE BUILDER WITH THE RELEVANT AUTHORITIES PRIOR TO THE COMMENCEMENT OF ANY BUILDING.

ADDRESS:
**3A WINDSOR CT CASTLE HILL (LOT 2)
LOT 92 DP 786466**
CLIENT:
MR. REHAN FIROZ & MR.SALMAN FIROZ

B	REVISION	14-05-2026
A	ISSUED FOR CC	08-02-2026
ISSUE	REVISION	DATE


ISSUE: TRUE NORTH:
B
CHECKED BY: D.NOBEL
DRAWN BY: A.PERVAIZ

DRAWING TITLE:
ELEVATIONS PART-2
DRAWING NUMBER: A04
SCALE: As indicated @ A3

ADA
design
ABN: 51 463 906 127
UNIT 1/128-130 VICTORIA STREET WERRINGTON NSW 2747
0431231255, info@adadesign.com.au
NOMINATED ARCHITECT: DENIS NOBEL (REG.12432)

HOMECERTS PTY LTD
Reference: 26234/01
Date: 29/05/2026
Construction Certificate (CC)
Dipak Ram
BDC 2686



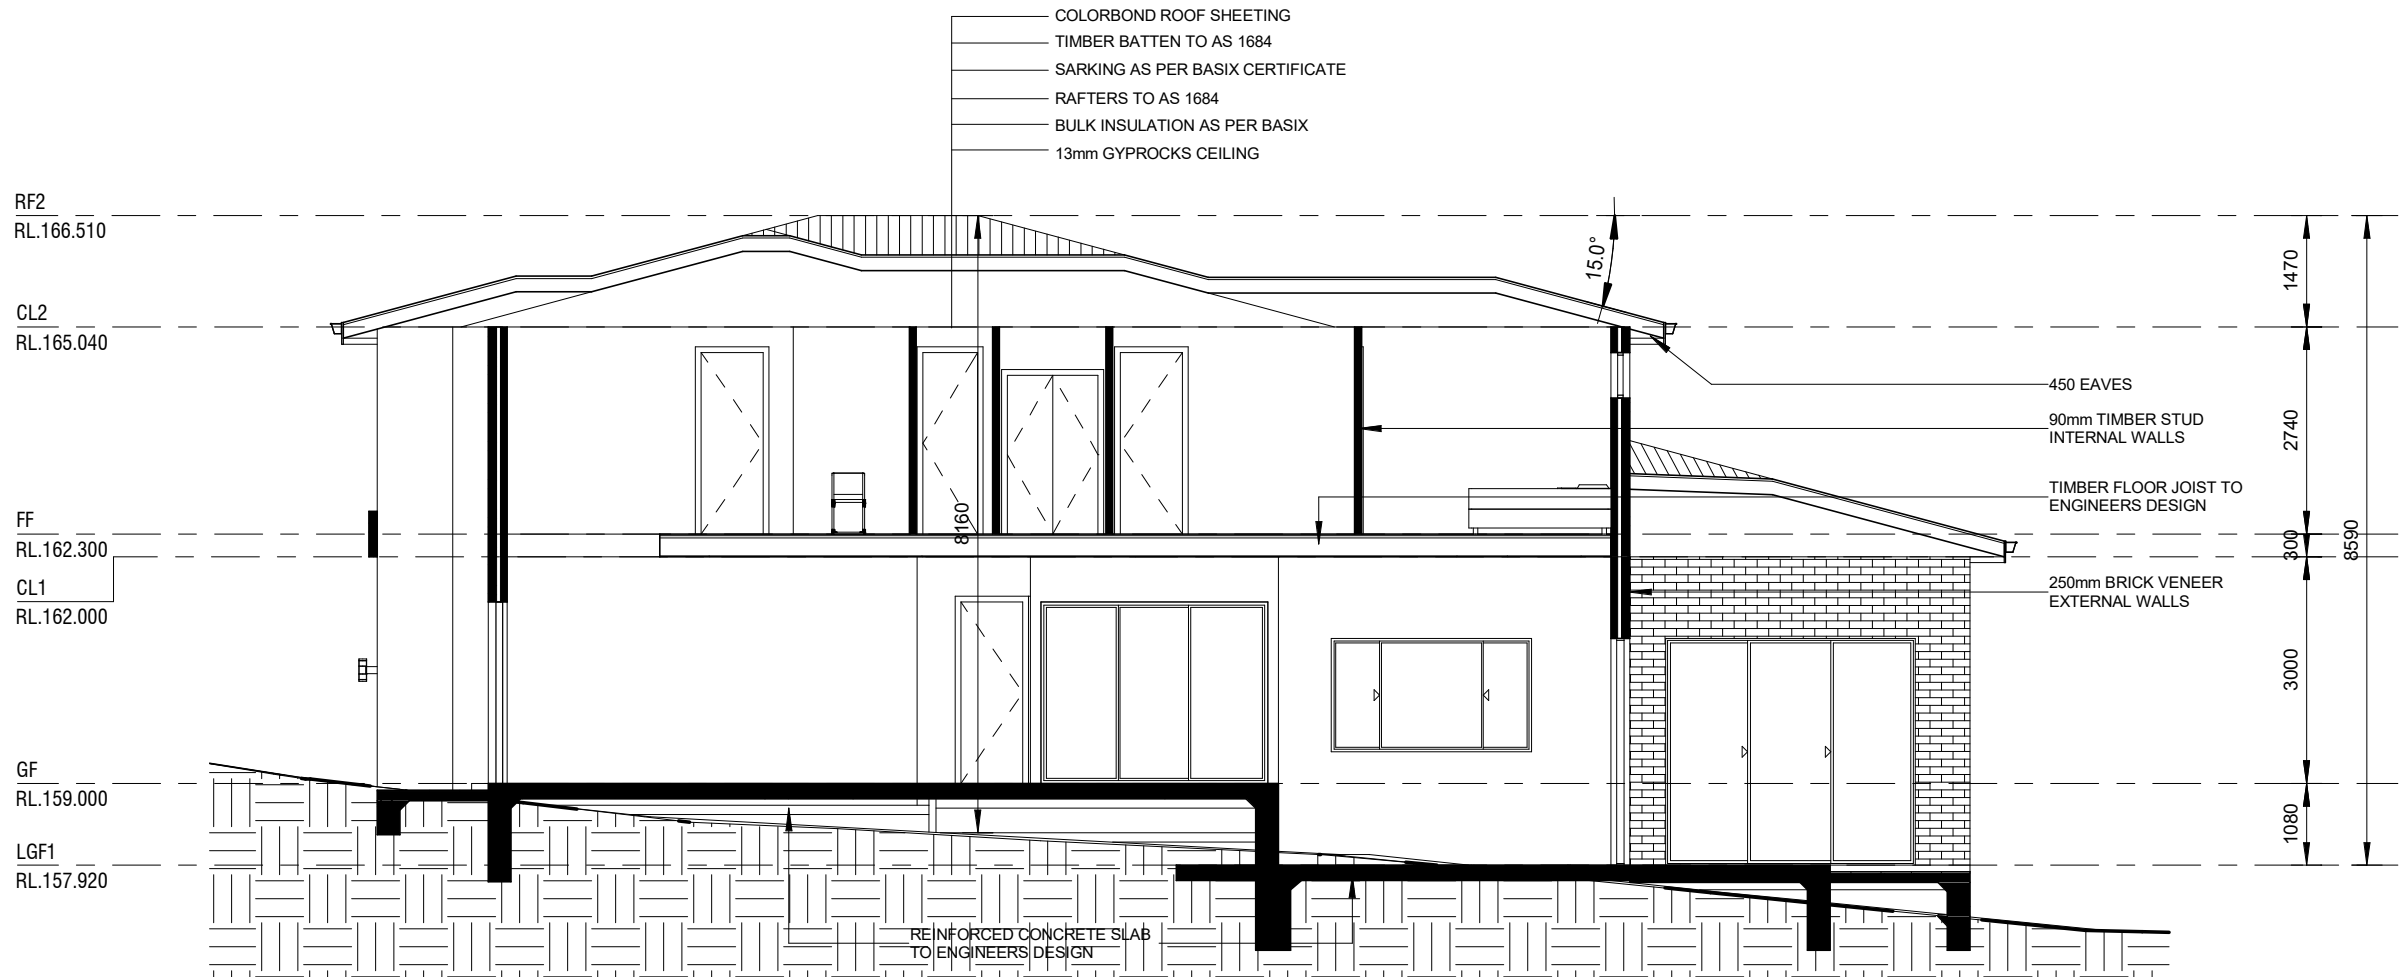

1
A05

SECTION - DW2
1 : 100

NOTES:

- ALL DIMENSIONS AND FLOOR AREAS TO BE VERIFIED PRIOR TO THE COMMENCEMENT OF ANY BUILDING WORK
- ANY DISCREPANCIES ARE TO BE CONFIRMED BY THE DESIGNER
- LEVELS SHOWN ARE APPROXIMATE UNLESS ACCOMPANIED BY REDUCED LEVELS BY A REGISTERED SURVEYOR
- FIGURED DIMENSIONS ARE TO BE TAKEN IN PREFERENCE TO SCALING
- ALL BOUNDARY CLEARANCE MUST BE VERIFIED BY THE SURVEYOR PRIOR TO THE COMMENCEMENT OF ANY BUILDING WORK
- WHERE ENGINEERING OR HYDRAULIC DRAWINGS ARE REQUIRED, SUCH MUST TAKE PREFERENCE TO THIS DRAWING
- STORMWATER TO BE CONNECTED AND DISCHARGED TO COUNCIL'S REQUIREMENTS AND TO AS 3500.3
- ALL SERVICES TO BE LOCATED AND VERIFIED BY THE BUILDER WITH THE RELEVANT AUTHORITIES PRIOR TO THE COMMENCEMENT OF ANY BUILDING

ADDRESS:
**3A WINDSOR CT CASTLE HILL (LOT 2)
LOT 92 DP 786466**

CLIENT:
MR. REHAN FIROZ & MR.SALMAN FIROZ

B	REVISION	14-05-2026
A	ISSUED FOR CC	08-02-2026
ISSUE	REVISION	DATE

ISSUE: TRUE NORTH:

B

CHECKED BY: D.NOBEL
DRAWN BY: A.PERVAIZ

DRAWING TITLE:
SECTION PART-1


DRAWING NUMBER: A05
SCALE: 1 : 100 @ A3

ADA
design

ABN: 51 463 906 127
UNIT 1/128-130 VICTORIA STREET WERRINGTON NSW 2747
0431231255, info@adadesign.com.au
NOMINATED ARCHITECT: DENIS NOBEL (REG.12432)

HOMECERTS PTY LTD
Reference: 26234/01
Date: 29/05/2026
Construction Certificate (CC)
Dipak Ram
BDC 2686



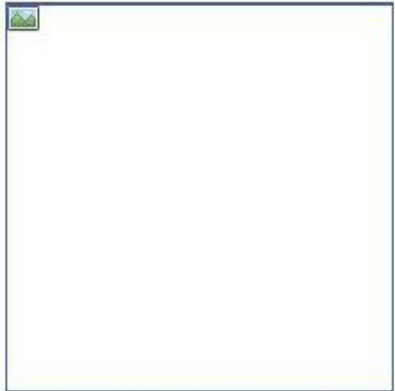

01: WHITE RENDER



02: WOOD FINISH



03: STONE FEATURE



04: ALUMINIUM WINDOWS
& DOORS



05: COLORBOND ROOF



06: FASCIA & GUTTER

1

SCHEDULE OF FINISHES

NOTES:

1. ALL DIMENSIONS AND FLOOR AREAS TO BE VERIFIED PRIOR TO THE COMMENCEMENT OF ANY BUILDING WORK

2. ANY DISCREPANCIES ARE TO BE CONFIRMED BY THE DESIGNER

3. LEVELS SHOWN ARE APPROXIMATE UNLESS ACCOMPANIED BY REDUCED LEVELS BY A REGISTERED SURVEYOR

4. FIGURED DIMENSIONS ARE TO BE TAKEN IN PREFERENCE TO SCALING

5. ALL BOUNDARY CLEARANCE MUST BE VERIFIED BY THE SURVEYOR PRIOR TO THE COMMENCEMENT OF ANY BUILDING WORK

6. WHERE ENGINEERING OR HYDRAULIC DRAWINGS ARE REQUIRED, SUCH MUST TAKE PREFERENCE TO THIS DRAWING

7. STORMWATER TO BE CONNECTED AND DISCHARGED TO COUNCIL'S REQUIREMENTS AND TO AS 3500.3

8. ALL SERVICES TO BE LOCATED AND VERIFIED BY THE BUILDER WITH THE RELEVANT AUTHORITIES PRIOR TO THE COMMENCEMENT OF ANY BUILDING

ADDRESS:
3A WINDSOR CT CASTLE HILL (LOT 2)
LOT 92 DP 786466

CLIENT:
MR. REHAN FIROZ & MR.SALMAN FIROZ

ISSUE	REVISION	DATE

ISSUE: TRUE NORTH:

B

CHECKED BY: D.NOBEL

DRAWN BY: A.PERVAIZ

DRAWING TITLE:
SCHEDULE OF FINISHES

DRAWING NUMBER: A10

SCALE: @ A3



ABN: 51 463 906 127
UNIT 1/128-130 VICTORIA STREET WERRINGTON NSW 2747
0431231255, info@adadesign.com.au
NOMINATED ARCHITECT: DENIS NOBEL (REG.12432)

HOMECERTS PTY LTD
Reference: 26234/01
Date: 29/05/2026
Construction Certificate (CC)
Dipak Ram
BDC 2686



WINDOW SCHEDULE - DW2				
Mark	Height	Width	Area	Level
W2.1	2100	2100	4.41 m²	GF
W2.2	600	2650	1.59 m²	GF
W2.3	3000	4500	13.50 m²	LGF1
W2.4	1500	2650	3.98 m²	LGF1
W2.5	1200	1810	2.17 m²	GF
W2.6	600	970	0.58 m²	GF
W2.7	2100	610	1.28 m²	FF
W2.8	2100	2100	4.41 m²	FF
W2.9	2100	610	1.28 m²	FF
W2.10	2100	1200	2.52 m²	FF
W2.11	2100	2100	4.41 m²	FF
W2.12	600	2650	1.59 m²	FF
W2.13	2100	1200	2.52 m²	FF
W2.14	600	970	0.58 m²	FF
W2.15	1200	1810	2.17 m²	FF
W2.16	600	2650	1.59 m²	FF
W2.17	600	2650	1.59 m²	FF
W2.18	600	1200	0.72 m²	FF
Grand total: 18			50.90 m²	

SLIDING DOOR SCHEDULE - DW2				
Mark	Height	Width	Area	Level
SD2.1	3000	3300	9.90 m²	LGF1
SD2.2	3000	3300	9.90 m²	LGF1
Grand total: 2			19.80 m²	

NOTES:

1. ALL DIMENSIONS AND FLOOR AREAS TO BE VERIFIED PRIOR TO THE COMMENCEMENT OF ANY BUILDING WORK.

2. ANY DISCREPANCIES ARE TO BE CONFIRMED BY THE DESIGNER.

3. LEVELS SHOWN ARE APPROXIMATE UNLESS ACCOMPANIED BY REDUCED LEVELS BY A REGISTERED SURVEYOR.

4. FIGURED DIMENSIONS ARE TO BE TAKEN IN PREFERENCE TO SCALING.

5. ALL BOUNDARY CLEARANCE MUST BE VERIFIED BY THE SURVEYOR PRIOR TO THE COMMENCEMENT OF ANY BUILDING WORK.

6. WHERE ENGINEERING OR HYDRAULIC DRAWINGS ARE REQUIRED, SUCH MUST TAKE PREFERENCE TO THIS DRAWING.

7. STORMWATER TO BE CONNECTED AND DISCHARGED TO COUNCIL'S REQUIREMENTS AND TO AS 3500.3.

8. ALL SERVICES TO BE LOCATED AND VERIFIED BY THE BUILDER WITH THE RELEVANT AUTHORITIES PRIOR TO THE COMMENCEMENT OF ANY BUILDING.

ADDRESS:

3A WINDSOR CT CASTLE HILL (LOT 2)

LOT 92 DP 786466

CLIENT:

MR. REHAN FIROZ & MR.SALMAN FIROZ

B	REVISION	14-05-2026
A	ISSUED FOR CC	08-02-2026
ISSUE	REVISION	DATE

ISSUE: TRUE NORTH:

B

CHECKED BY: D.NOBEL

DRAWN BY: A.PERVAIZ

DRAWING TITLE:

WINDOWS & DOOR SCHEDULE

DRAWING NUMBER: A11

SCALE: @ A3

ADA
design

ABN: 51 463 906 127
UNIT 1/128-130 VICTORIA STREET WERRINGTON NSW 2747
0431231255, info@adadesign.com.au
NOMINATED ARCHITECT: DENIS NOBEL (REG.12432)