


DEVELOPMENT CHECKLIST
LOW RISE HOUSING DIVERSITY DESIGN GUIDE
(FOR COMPLYING DEVELOPEMENT)


MIN LOT SIZE	STANDARD 550 m2	PROPOSED 695.5 m2
MIN LOT WIDTH	15.0 m	15.24 m
HEIGHT OF BUILDINGS (LEP)	8.5 m	8.50 m
NUMBER OF STOREYS	2	2
MAXIMUM GROSS FLOOR AREA	473.9 m2	361.6 m2
MIN LANDSCAPE AREA	247.8 m2	296.8 m2
FRONT LANDSCAPE	25%	54%
REAR LANDSCAPE	123.9 m2	235.6 m2
PRIVATE OPEN SPACE	16.0 m2	132 m2
MIN DWELLING SIZE	132 m2	174.3 m2
MIN LIVING/DINING AREA	28 m2	34 m2
CEILING HEIGHTS	2700mm	2740mm
STORAGE AREA	10 m3	10.6 m3
CARPARKING	1 SPACE	1 SPACE
FRONT SETBACK	5.81 m	5.82 m
SECONDARY SETBACK	2.0 m	N/A
REAR GROUND FLOOR SETBACK	8.0 m	22.16 m
REAR FIRST FLOOR SETBACK	3.0 m	15.46 m
GROUND FLOOR SIDE SETBACK	0.9m	1.27 m
FIRST FLOOR SIDE SETBACK	1.25m	1.27 m



DEMOLITION OF EXISTING STRUCTURES
PROPOSED 2 LOT SUB-DIVISION & THE
CONSTRUCTION OF 2 SEMI-DETACHED DWELLINGS

LOT 100 DP 15577
64 OAKS AVENUE
SHELLY BEACH

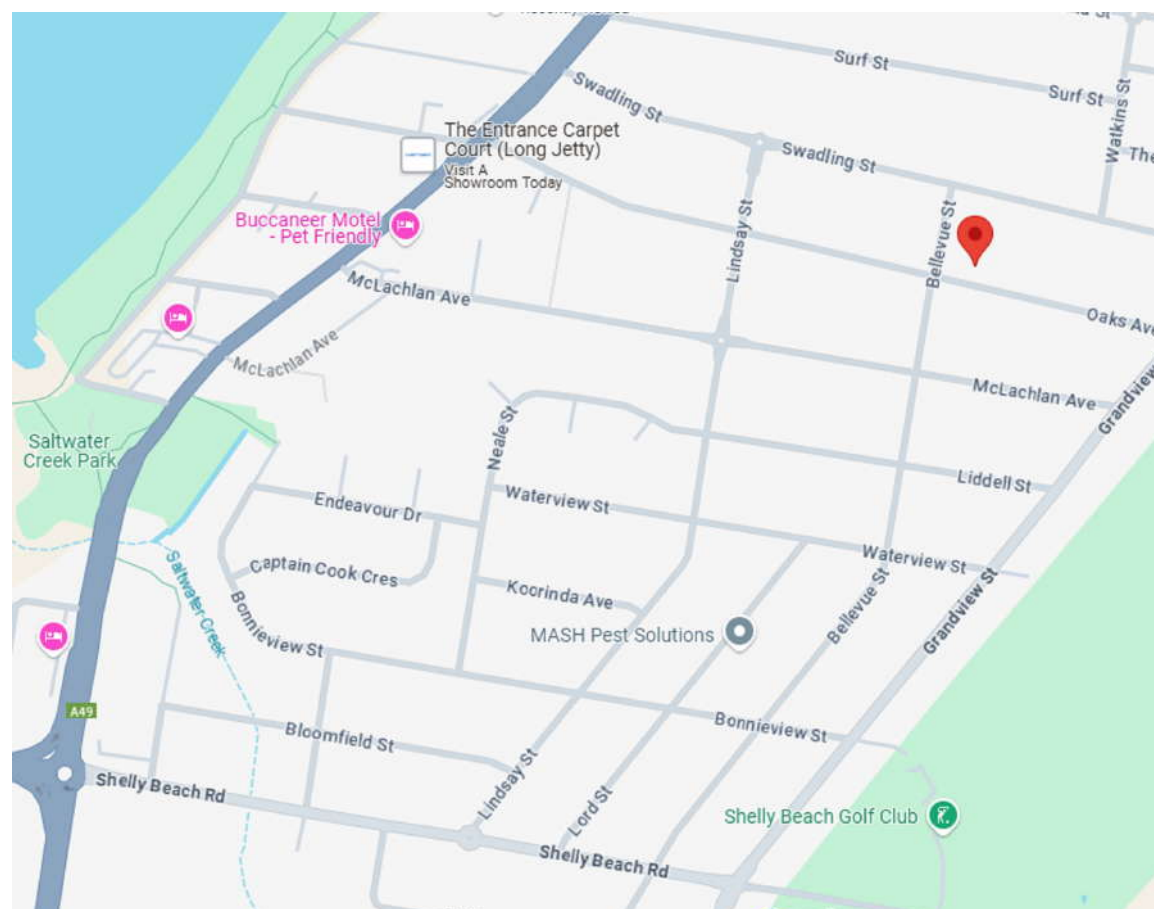

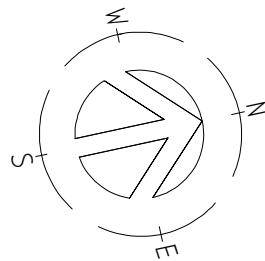

All construction to be in
accordance with NCC
severe marine environment

NOTE:
- SITE LEVELS SHOWN ARE APPROXIMATE ONLY AND SUBJECT TO SITE CONDITIONS
- FINAL FINISHED FLOOR LEVELS TO BE DETERMINED ON SITE BY BUILDER


LOCATION OF NEW DOWNPIPES SHOWN ARE SUBJECT TO VERIFICATION BY THE BUILDER DURING CONSTRUCTION. DOWNPIPES, SURFACE INLETS & KERB OUTLET LOCATIONS MAY VARY PROVIDING THE INTENT OF THE STORMWATER DESIGN IS MAINTAINED.

ANY EXISTING STREET TREE AND VERGE PLANTING TO BE PROTECTED DURING CONSTRUCTION

SITE NOTES
- Do not scale of the drawings unless otherwise stated as written dimensions will take preference over scaling
- All dimensions and levels are to be checked and verified by the CONTRACTOR on site before the commencement of any works, all dimensions and levels are subject to final survey and set-out. Discrepancies to be reported to the designer prior to commencement of any works
- Where Engineers drawings are required such must take preference over this set of drawings
- Contours have been interpolated from the spot heights taken and are approximate only
- Finished site levels, banks excavations & filling may vary due to site conditions. Adjustments while complying with council requirements remain at the discretion of the builder
- All boundary clearances are to be verified by survey before any work
- All services to be located and verified by the Builder with the relevant authorities prior to any work commencing
- All work to be carried out in accordance with the Building Code of Australia, all Local and State Government Ordinances, relevant Australian Standards, Electricity and Water Authorities Regulations and all other relevant Authorities.

LEGEND

	Gate
	Hydrant
	Fence
	Sewer line
	Telecomms
	Water
	Drainage pit
	Tap
	Door
	Floor Level
	Window Head
	Invert Level
	Lip of Roof Gutter
	Ridge/Roof Level
	Window Sill
	Surface Level
	Window
	Telecomms pit
	Water meter

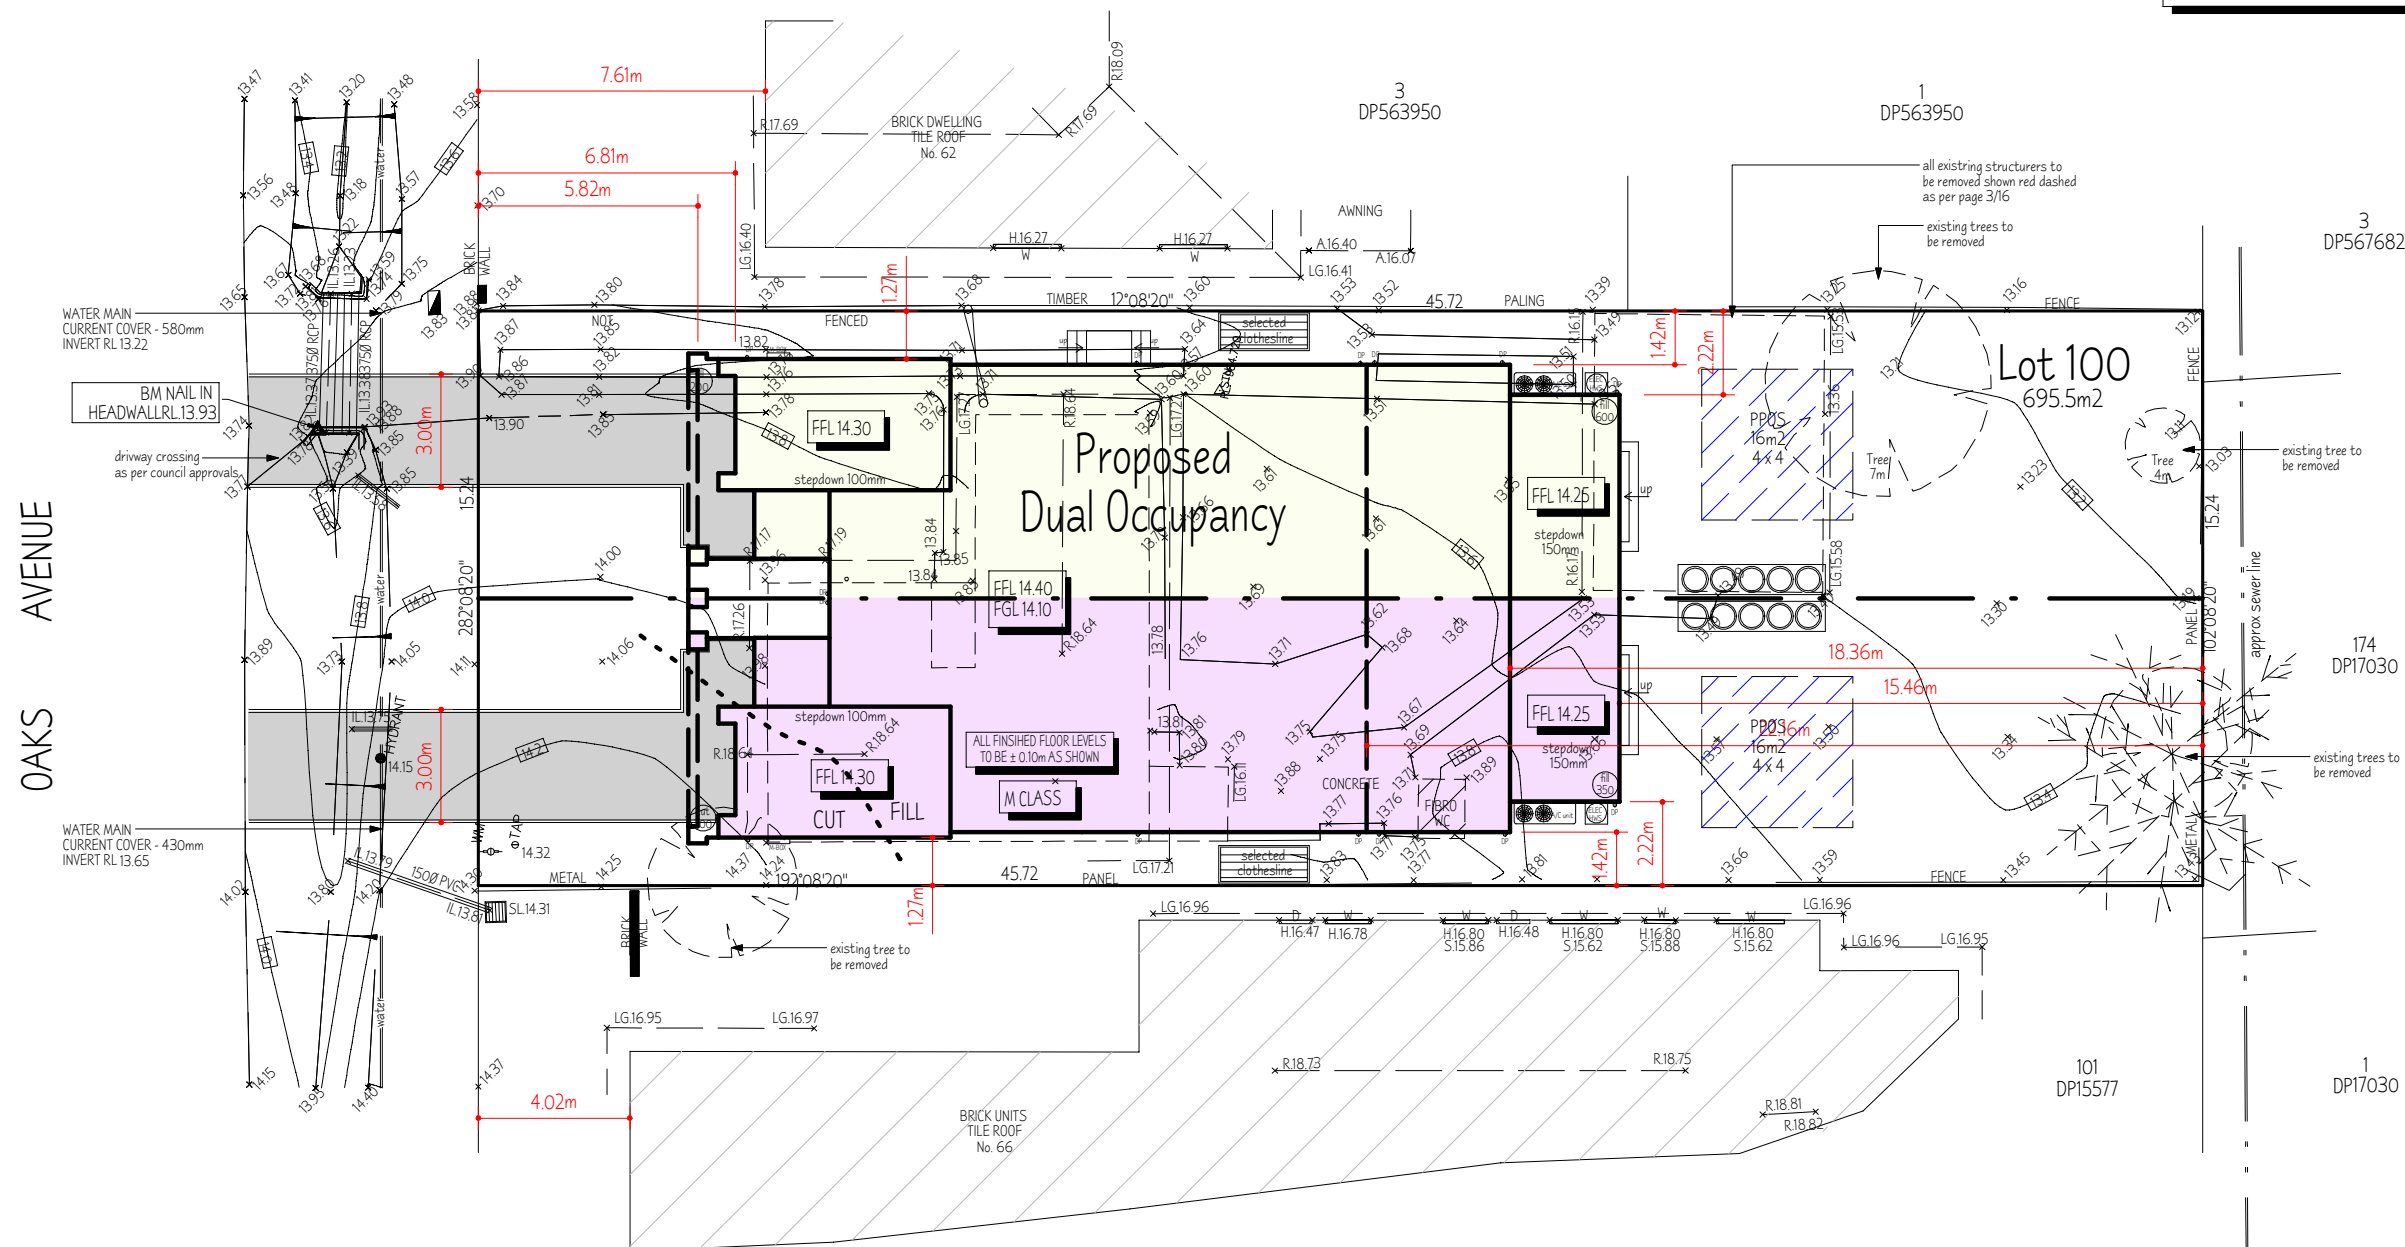

SITE PLAN

scale 1:200

PROPOSED DUAL OCCUPANCY




client
AKABE HOLDINGS & ANTANGA

project
LOT 100 DP 15577
64 OAKS AVENUE
SHELLY BEACH


scale 1:200 drawing title SITE PLAN

drawn J.S. job no. REW ---


date 17/06/26 drawing no. 2/15 issue E.

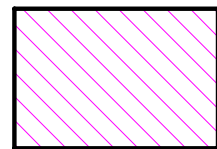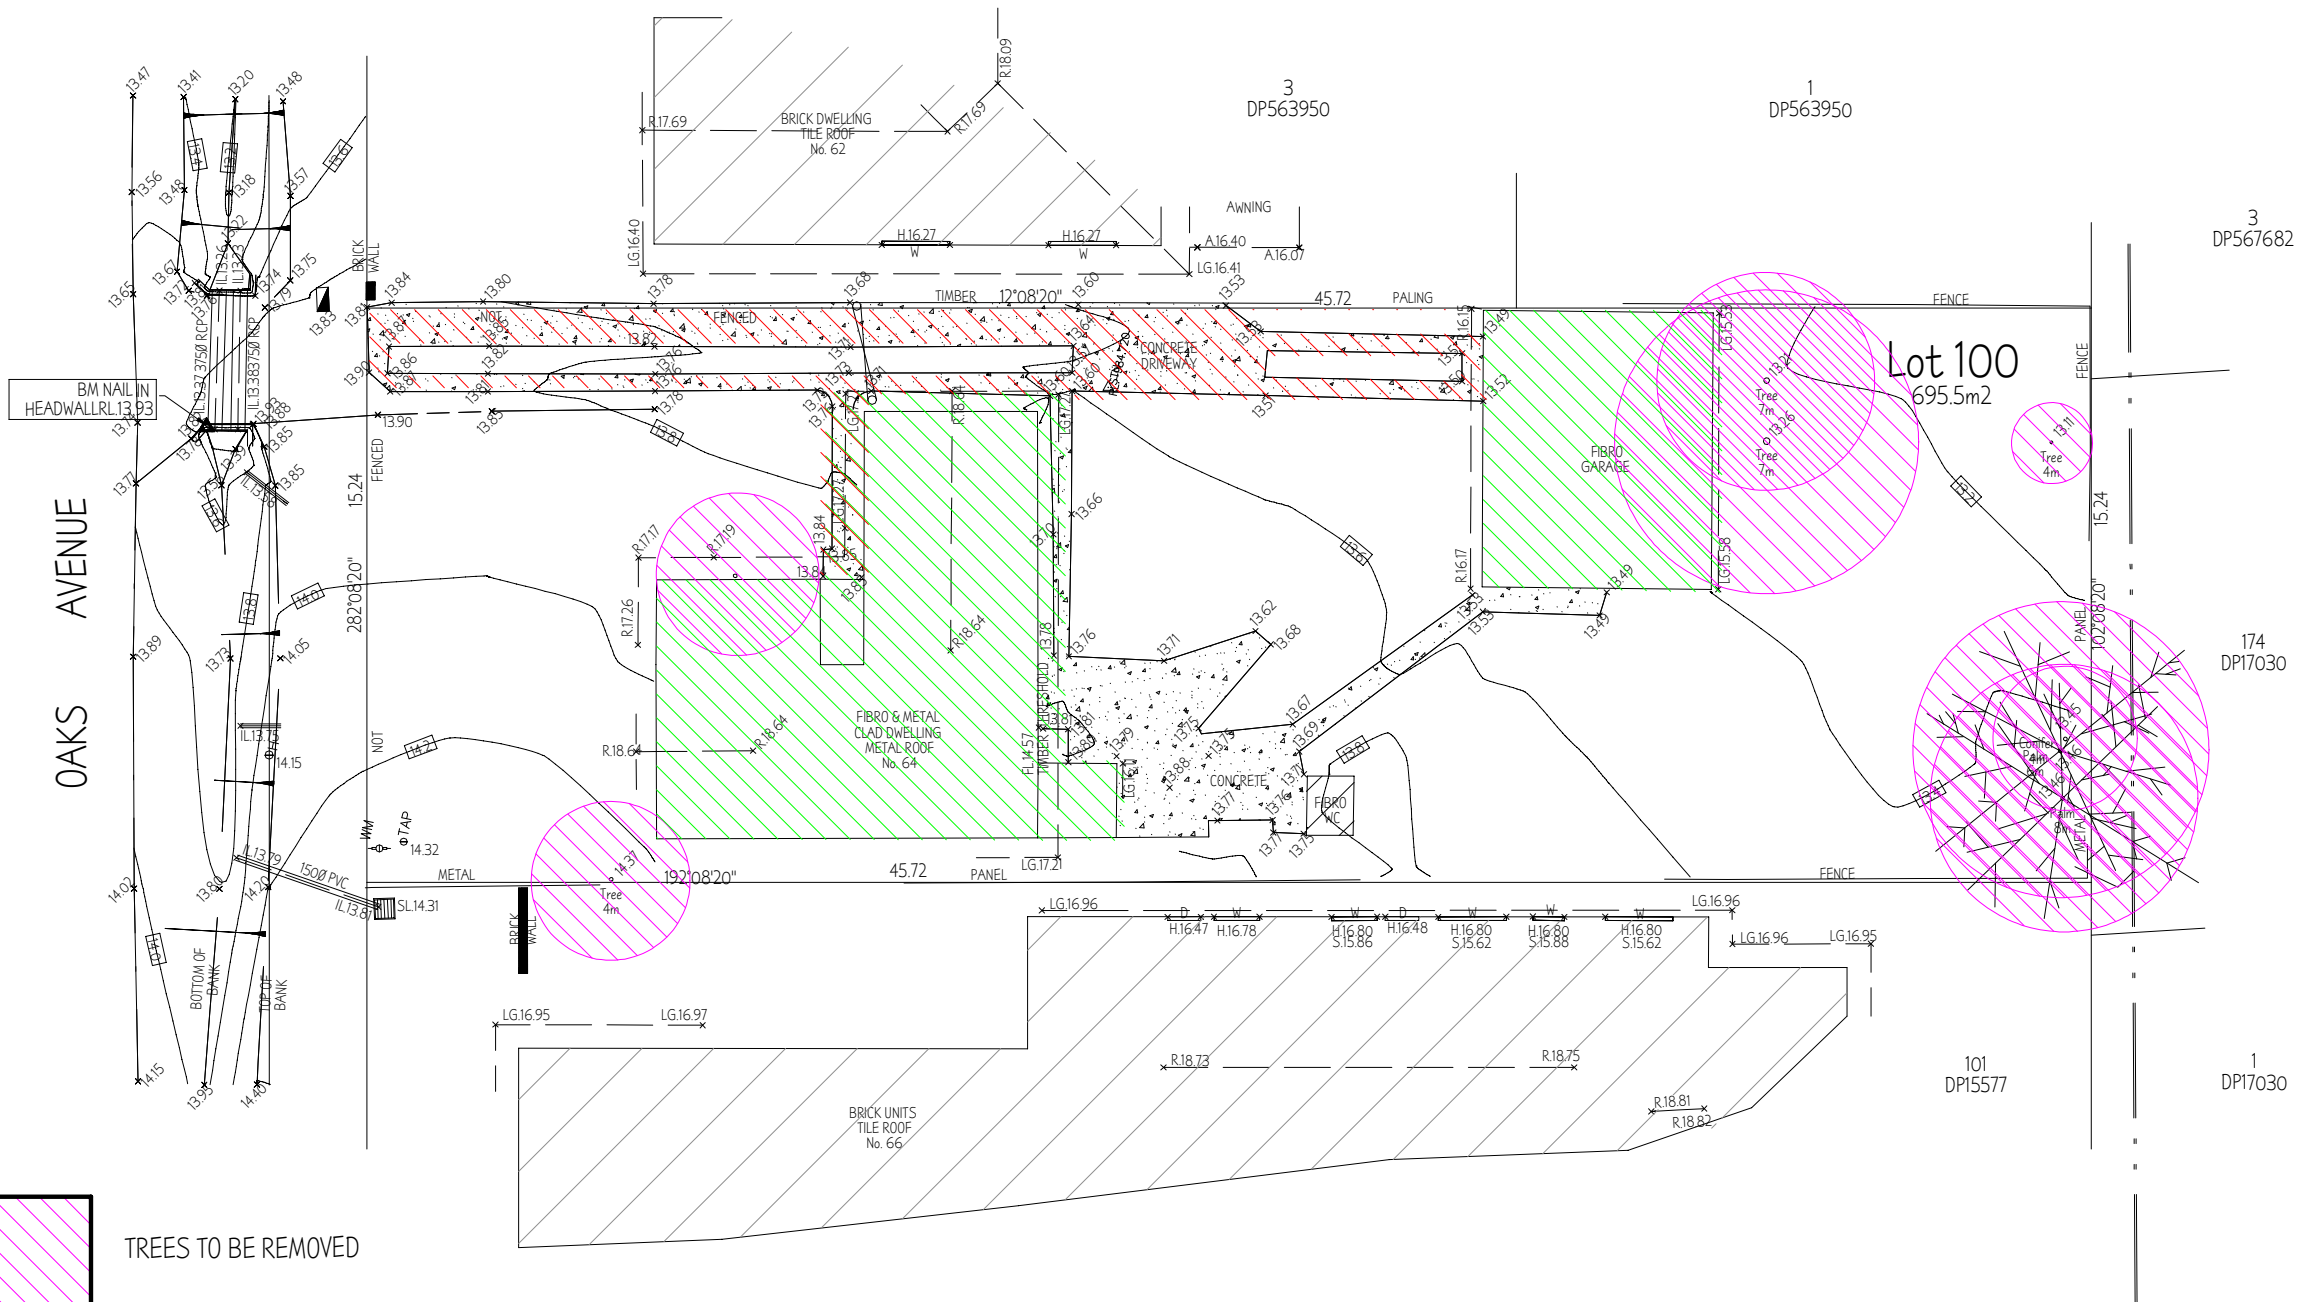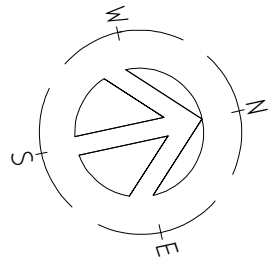

TREES TO BE REMOVED

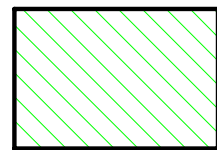

STRUCTURES REMOVED AS PER
AS2601 - 2001 DEMOLITION CODE

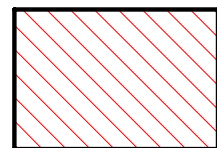

PATHS, DRIVEWAYS REMOVED AS PER
AS2601 - 2001 DEMOLITION CODE



DEMOLITION PLAN

scale 1:200

GENERAL NOTES
- Do not scale of the drawings unless otherwise stated as written dimensions will take preference over scaling
- All dimensions and levels are to be checked and verified by the CONTRACTOR on site before the commencement of any works, all dimensions and levels are subject to final survey and set-out. Discrepancies to be reported to the designer prior to commencement of any works
- Where Engineers drawings are required such must take preference over this set of drawings
- All work to be carried out in accordance with the Building Code of Australia, all Local and State Government Ordinances, relevant Australian Standards, Electricity and Water Authorities Regulations and all other relevant Authorities.

PROPOSED DUAL OCCUPANCY


client
AKABE HOLDINGS & ANTANGA

project
LOT 100 DP 15577
64 OAKS AVENUE
SHELLY BEACH


scale 1:200 drawing title
DEMOLITION PLAN

drawn J.S. job no. REW ---

date 17/06/26 drawing no. 3/15 issue E.

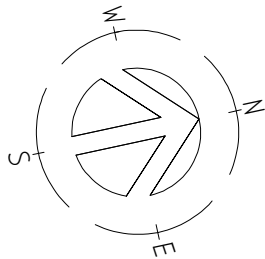

OAKS AVENUE

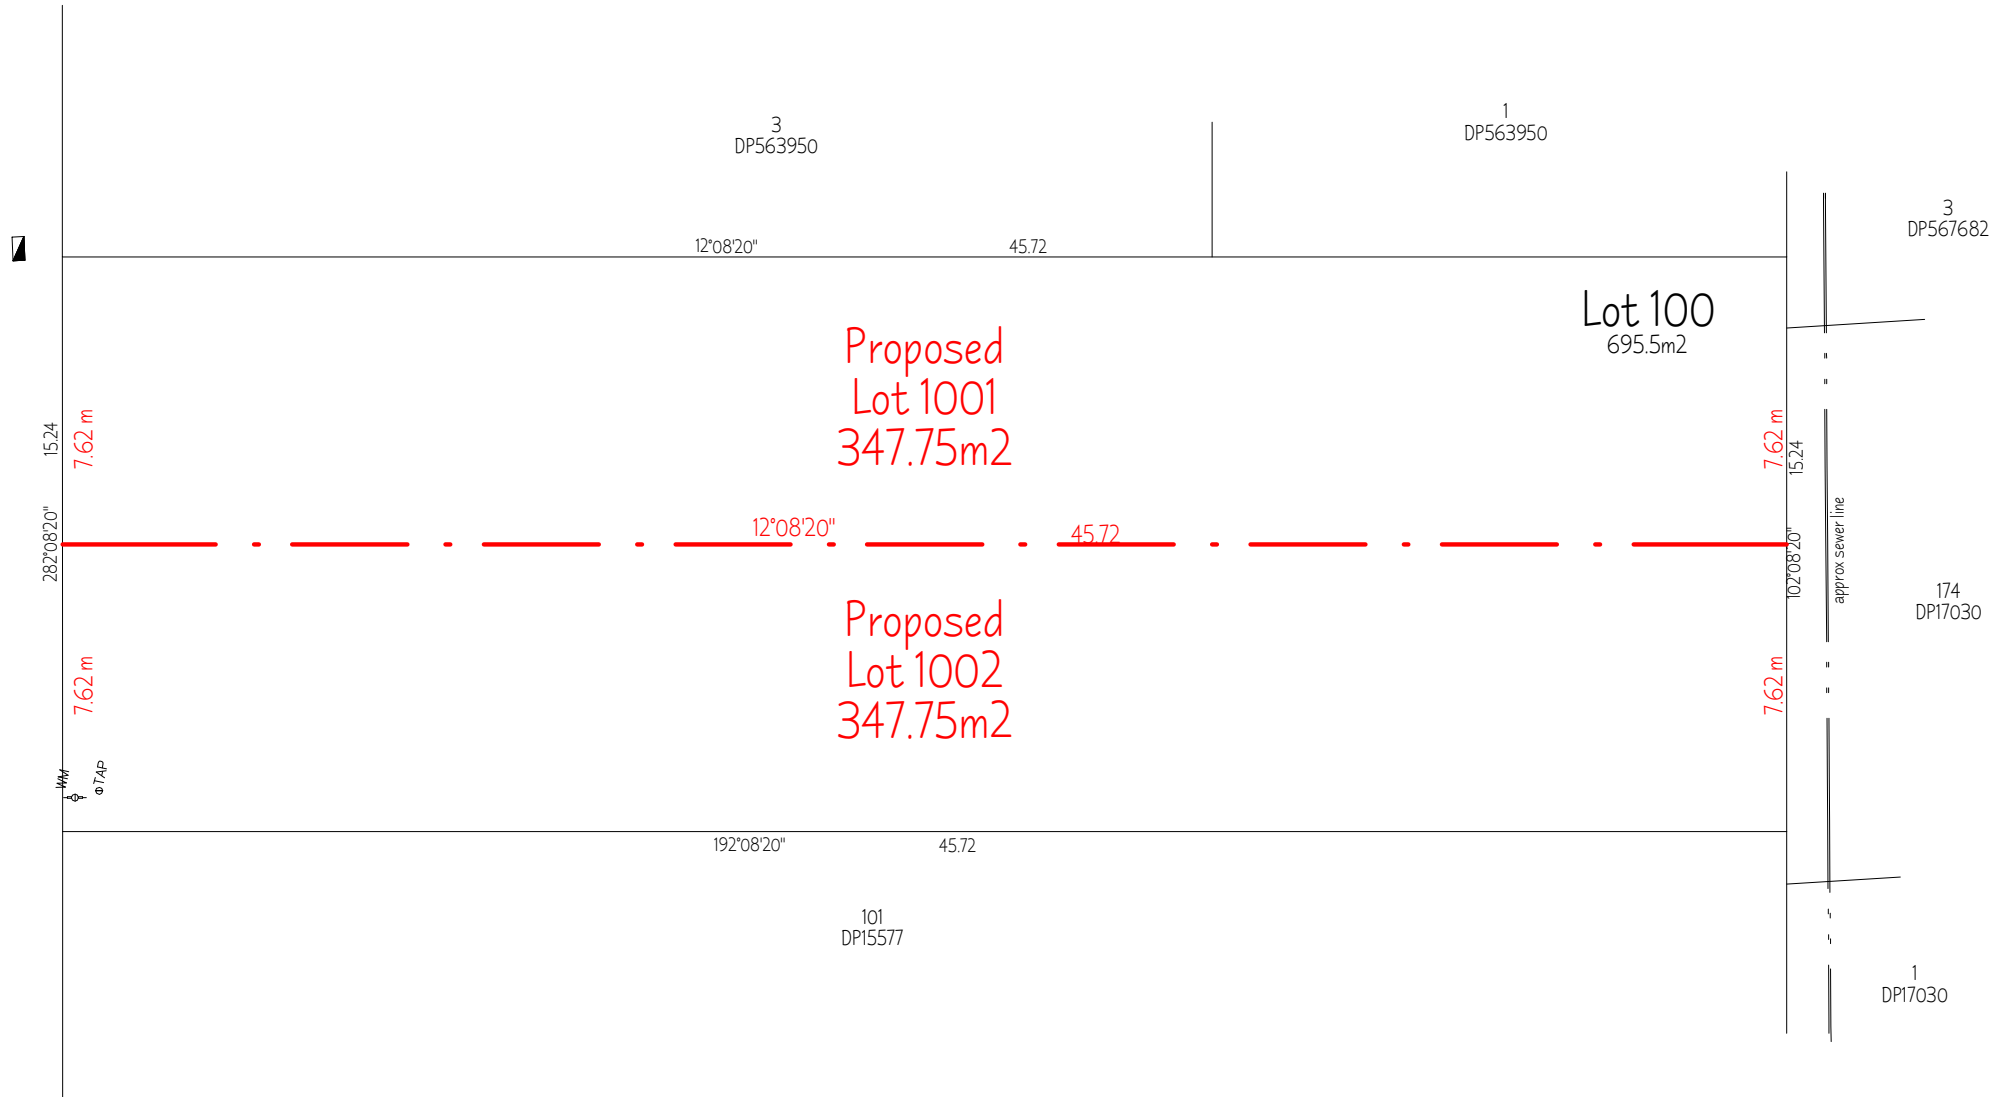

SUBDIVISION PLAN
scale 1 : 200


NOTE:
- FINAL SUB-DIVISION PLANS AS PER
FUTURE PLANS AND CALCULATIONS
BY REGISTERED SURVEYOR

GENERAL NOTES
- Do not scale of the drawings unless otherwise stated as
written dimensions will take preference over scaling
- All dimensions and levels are to be checked and verified
by the CONTRACTOR on site before the commencement of any works,
all dimensions and levels are subject to final survey and set-out.
Discrepancies to be reported to the designer prior to commencement
of any works
- Where Engineers drawings are required such must take
preference over this set of drawings
- All work to be carried out in accordance with the
Building Code of Australia, all Local and State Government
Ordinances, relevant Australian Standards, Electricity and
Water Authorities Regulations and all other relevant Authorities.

PROPOSED DUAL OCCUPANCY





client
AKABE HOLDINGS & ANTANGA
project
LOT 100 DP 15577
64 OAKS AVENUE
SHELLY BEACH

scale	1:200	drawing title	SUB-DIDVISION PLAN
drawn	J.S	job no.	REW ---
date	17/06/26	drawing no.	4/15
		issue	E.

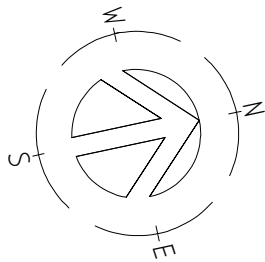





- SEDIMENTATION / SITE CONTROL NOTES
- All Erosion & Sedimentation control measures, including revegetation and storage of soil and topsoil shall be implemented to the standards of the Soil Conservation Of NSW
 - All Erosion & Sedimentation controls measures to be inspected and maintained daily.
 - Roads and Footpaths to be swept and kept clean daily.
 - All disturbed areas to be minimized.
 - All stockpiles to be clear of Drains, Gutters & Footpaths.
 - Drainage to be connected to Stormwater as soon as possible.
 - Filter shall be constructed by stretching a filter fabric (Propex or Approved Equivalent) between post at 3.0m centres. Fabric shall be buried 150mm along it's lower edge
 - 2.0m high chain mesh fence around tree preservation zones to remain intact until all construction on site is completed

- GENERAL NOTES
- Do not scale of the drawings unless otherwise stated as written dimensions will take preference over scaling
 - All dimensions and levels are to be checked and verified by the CONTRACTOR on site before the commencement of any works, all dimensions and levels are subject to final survey and set-out. Discrepancies to be reported to the designer prior to commencement of any works
 - Where Engineers drawings are required such must take preference over this set of drawings
 - All work to be carried out in accordance with the Building Code of Australia, all Local and State Government Ordinances, relevant Australian Standards, Electricity and Water Authorities Regulations and all other relevant Authorities.

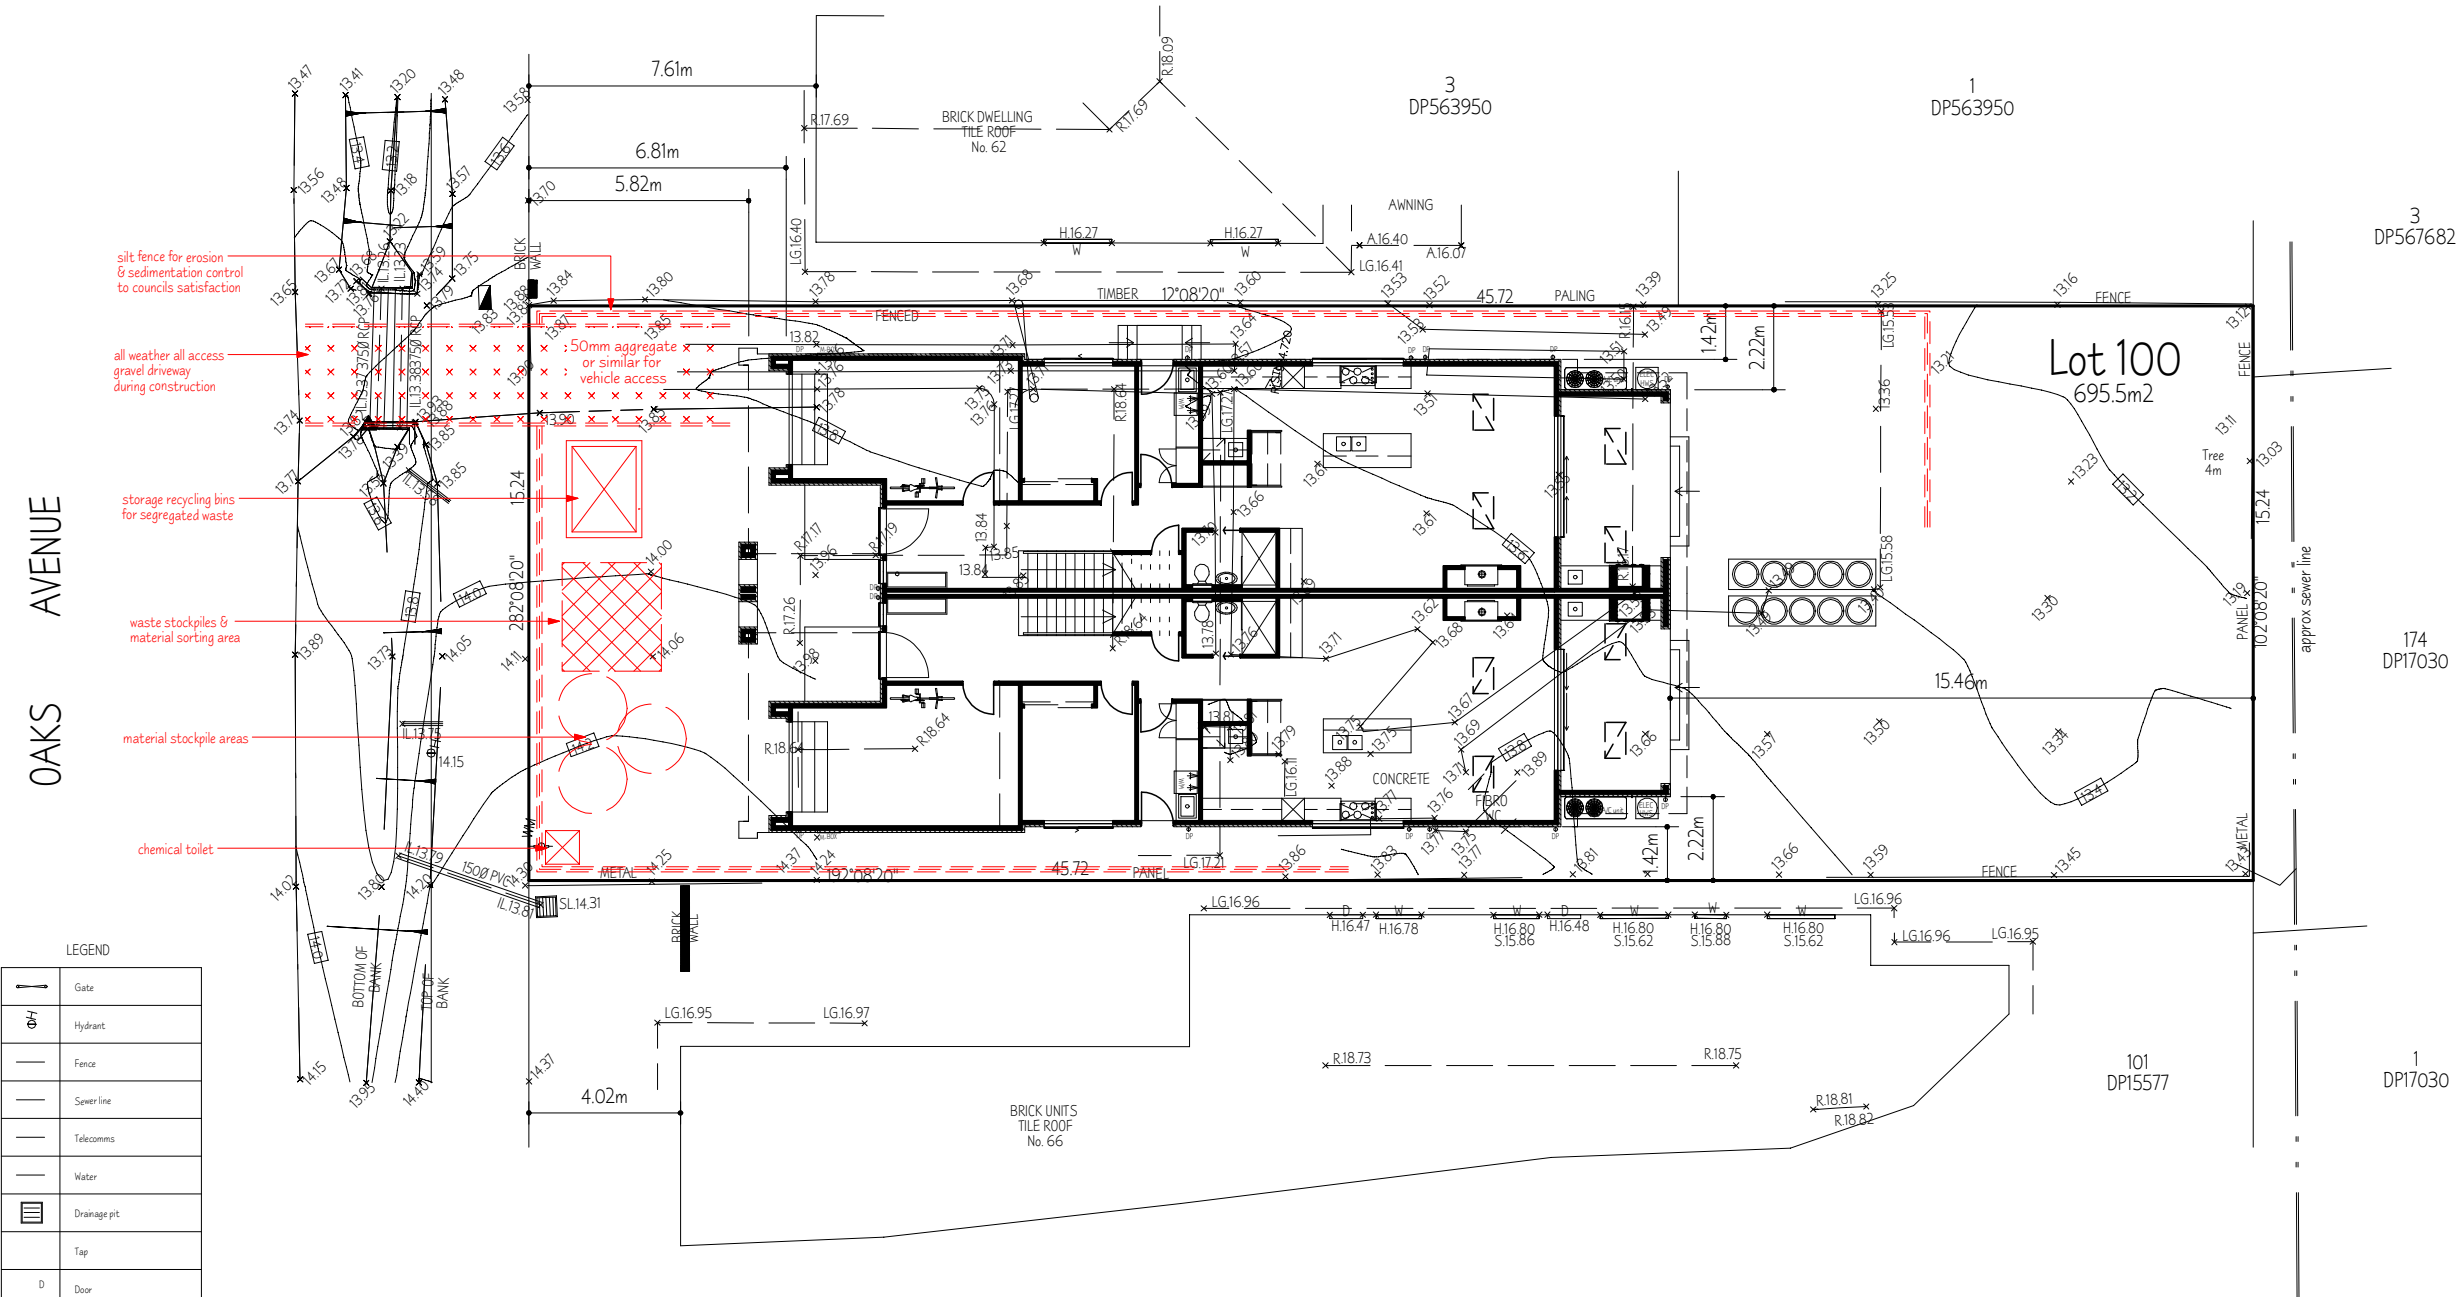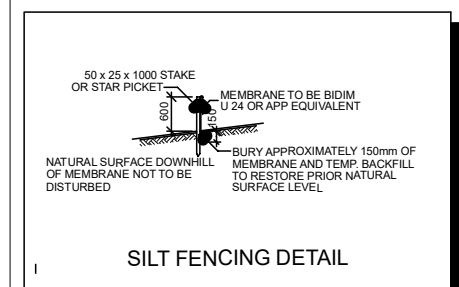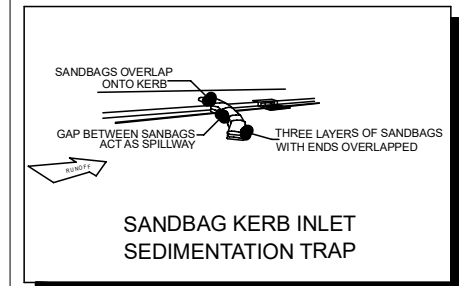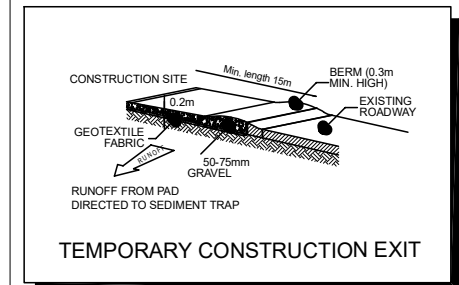

SITE MANAGEMENT PLAN
scale 1:200

client	AKABE HOLDINGS & ANTANGA		
project	LOT 100 DP 15577 64 OAKS AVENUE SHELLY BEACH		
scale	1:200	drawing title	SITE MANAGEMENT
drawn	J.S	job no.	REW ---
date	17/06/26	drawing no.	5/15
		issue	E.

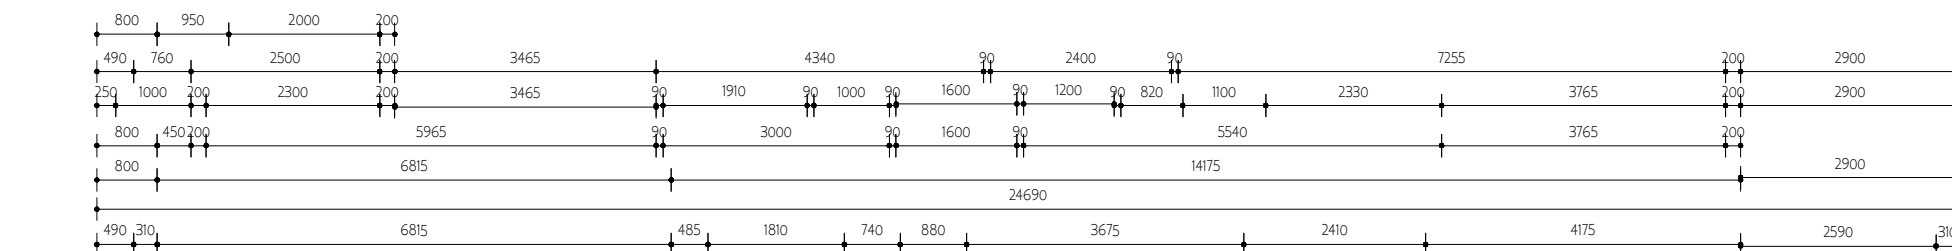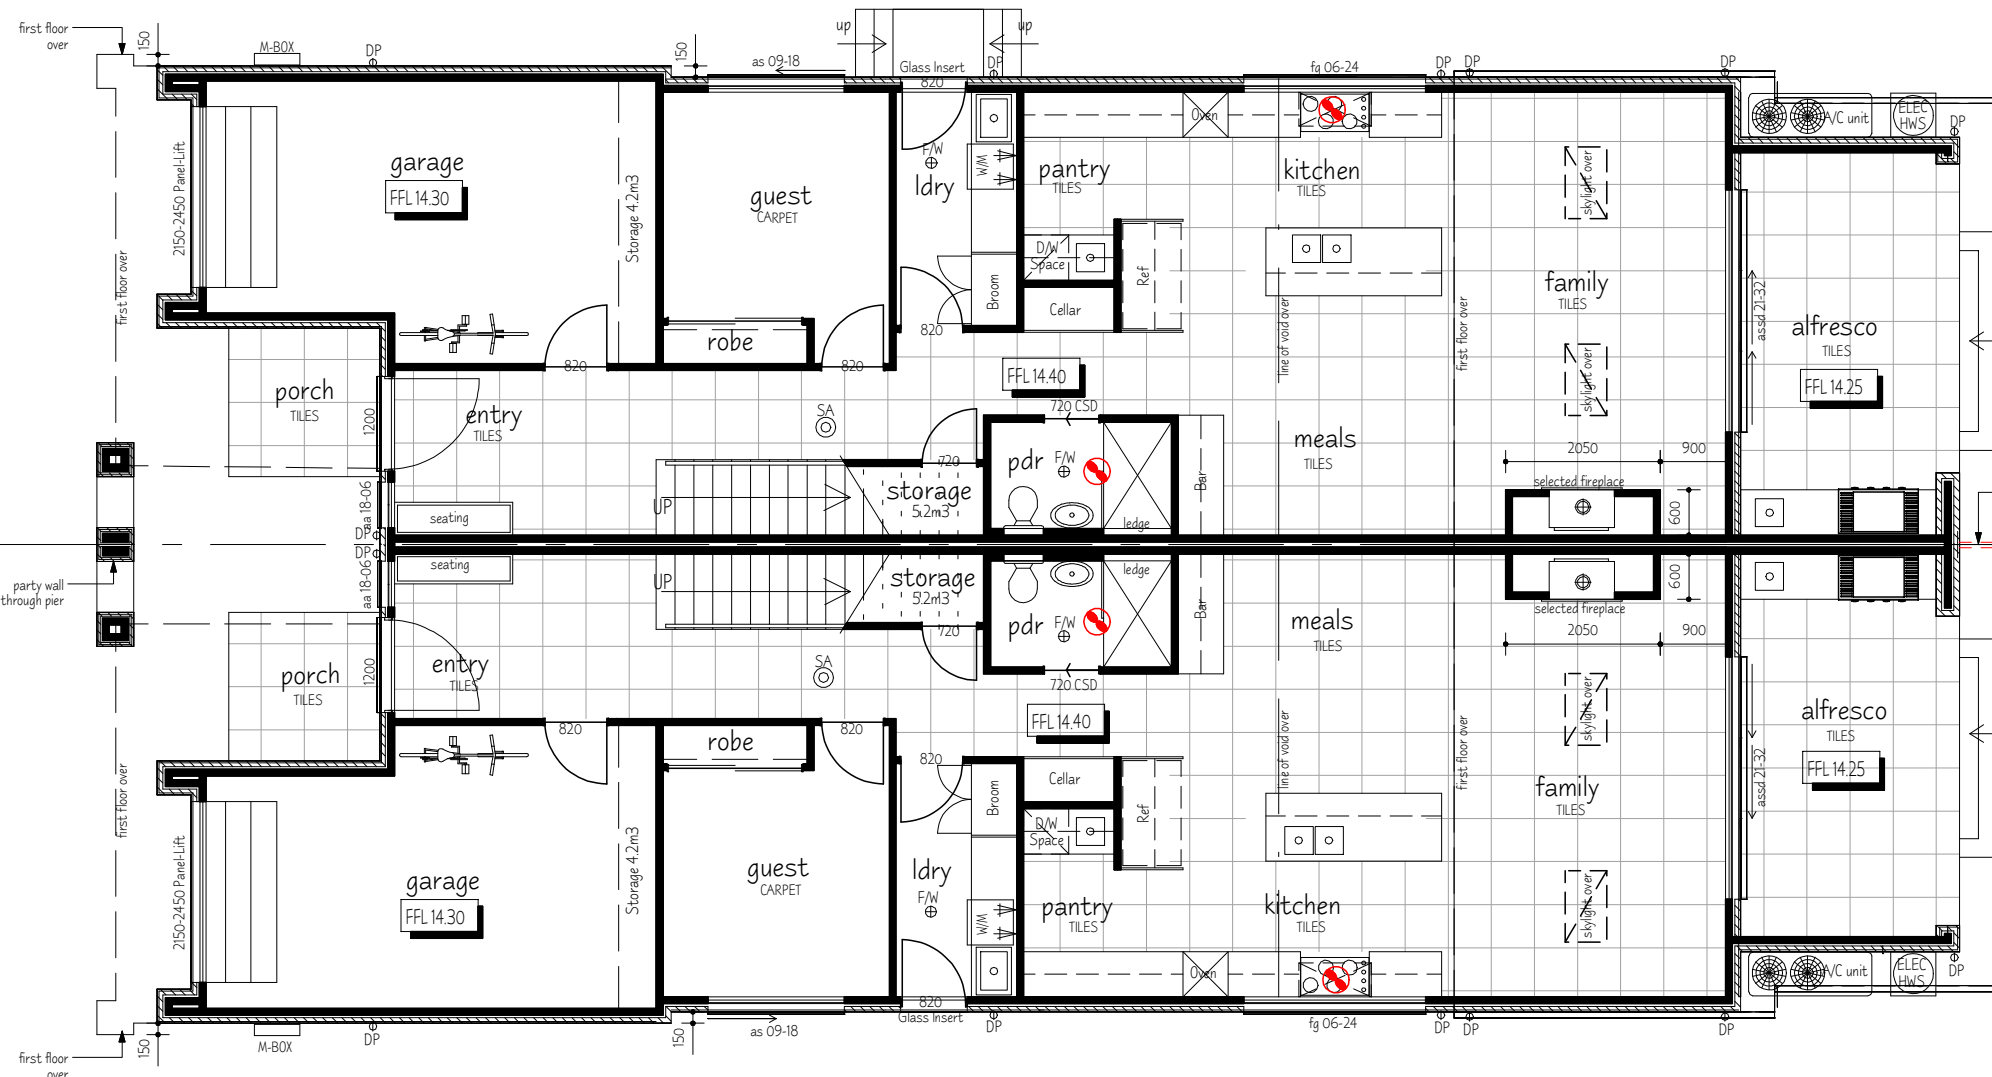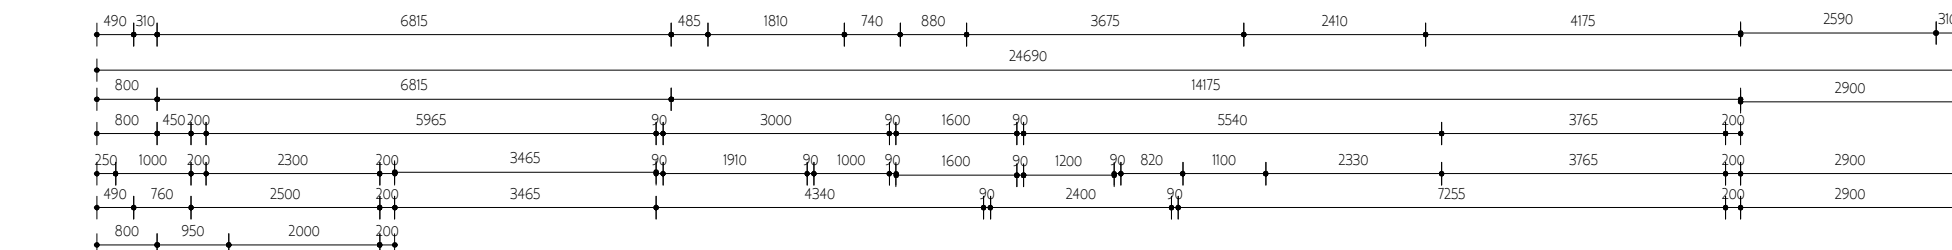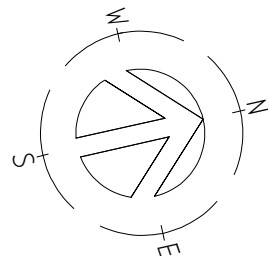

Itemised Floor Areas:	Totals:
ground floor:	198.0 m ²
first floor	215.4 m ²
garage:	45.2 m ²
porch / balcony	7.2 m ²
alfresco	31.4 m ²
total floor area:	497.2 m ²

GROUND FLOOR PLAN
scale 1 : 100

GENERAL NOTES
- Do not scale of the drawings unless otherwise stated as written dimensions will take preference over scaling
- All dimensions and levels are to be checked and verified by the CONTRACTOR on site before the commencement of any works, all dimensions and levels are subject to final survey and set-out. Discrepancies to be reported to the designer prior to commencement of any works.
- Where Engineers drawings are required such must take preference over this set of drawings
- All work to be carried out in accordance with the Building Code of Australia, all Local and State Government Ordinances, relevant Australian Standards, Electricity and Water Authorities Regulations and all other relevant Authorities concerned.


PROPOSED DUAL OCCUPANCY		scale	1:100	drawing title		FLOOR PLANS
client	AKABE HOLDINGS & ANTANGA		drawn	J.S	job no.	REW ---
project	LOT 100 DP 15577 64 OAKS AVENUE SHELLY BEACH		date	17/06/26	drawing no.	6/15
				issue		E.

ROOF TO BE VENTILATED AS PER
HOUSING PROVISIONS 10.8.3
CONDENSATION MANAGEMENT

VENTILATION TO BE AS PER
H4D9 PART 10.6 VENTILATION

MECHANICAL VENTILATION TO BE
DISCHARGED TO OUTSIDE AIR AS PER
H4D9 PART 10.8 - CONDENSATION MANAGEMENT
25 L/s FOR BATHROOMS
40 L/s FOR KITCHEN OR LAUNDRY

WATERPROOFING AS PER AS 3740.2021 &
HP 10.2 2022
WET AREA FALLS ARE TO BE IN
ACCORDANCE WITH HP 10.2.12 AND NCC H4D2






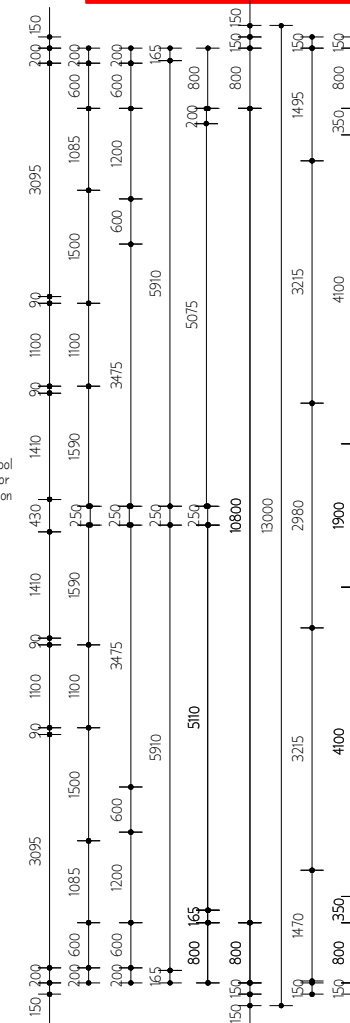


LOCATION OF NEW DOWNPIPES SHOWN
ARE SUBJECT TO VERIFICATION
BY THE BUILDER DURING CONSTRUCTION.
DOWNPIPES, SURFACE INLETS & KERB OUTLET
LOCATIONS MAY VARY PROVIDING COMPLIANCE
WITH AS/NZS 3500.3:2015 IS MAINTAINED.

VANITY SIZES SHOWN ARE APPROXIMATE
ONLY AND ARE TO BE CONFIRMED ON
SITE PRIOR TO INSTALLATION

- SHOWER RECESSES TO BE
350mm HIGH x 650mm WIDE
AT 1200mm ABOVE FFL

All construction to be in
accordance with NCC
severe marine environment

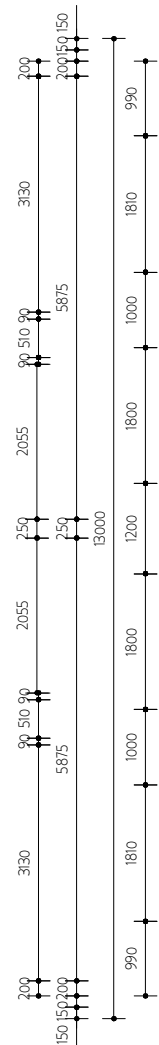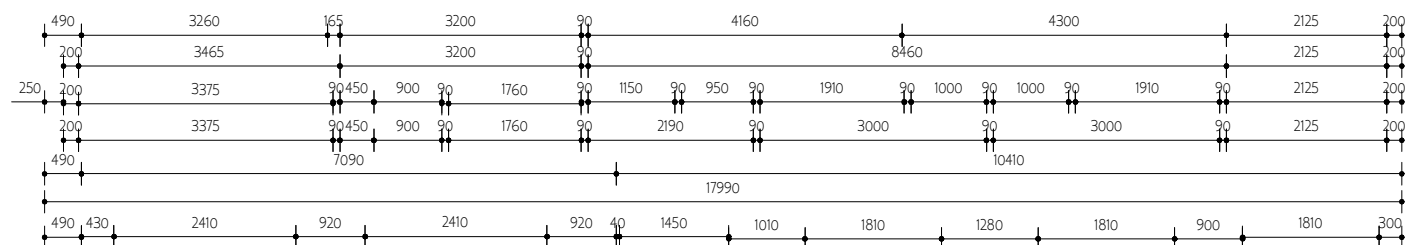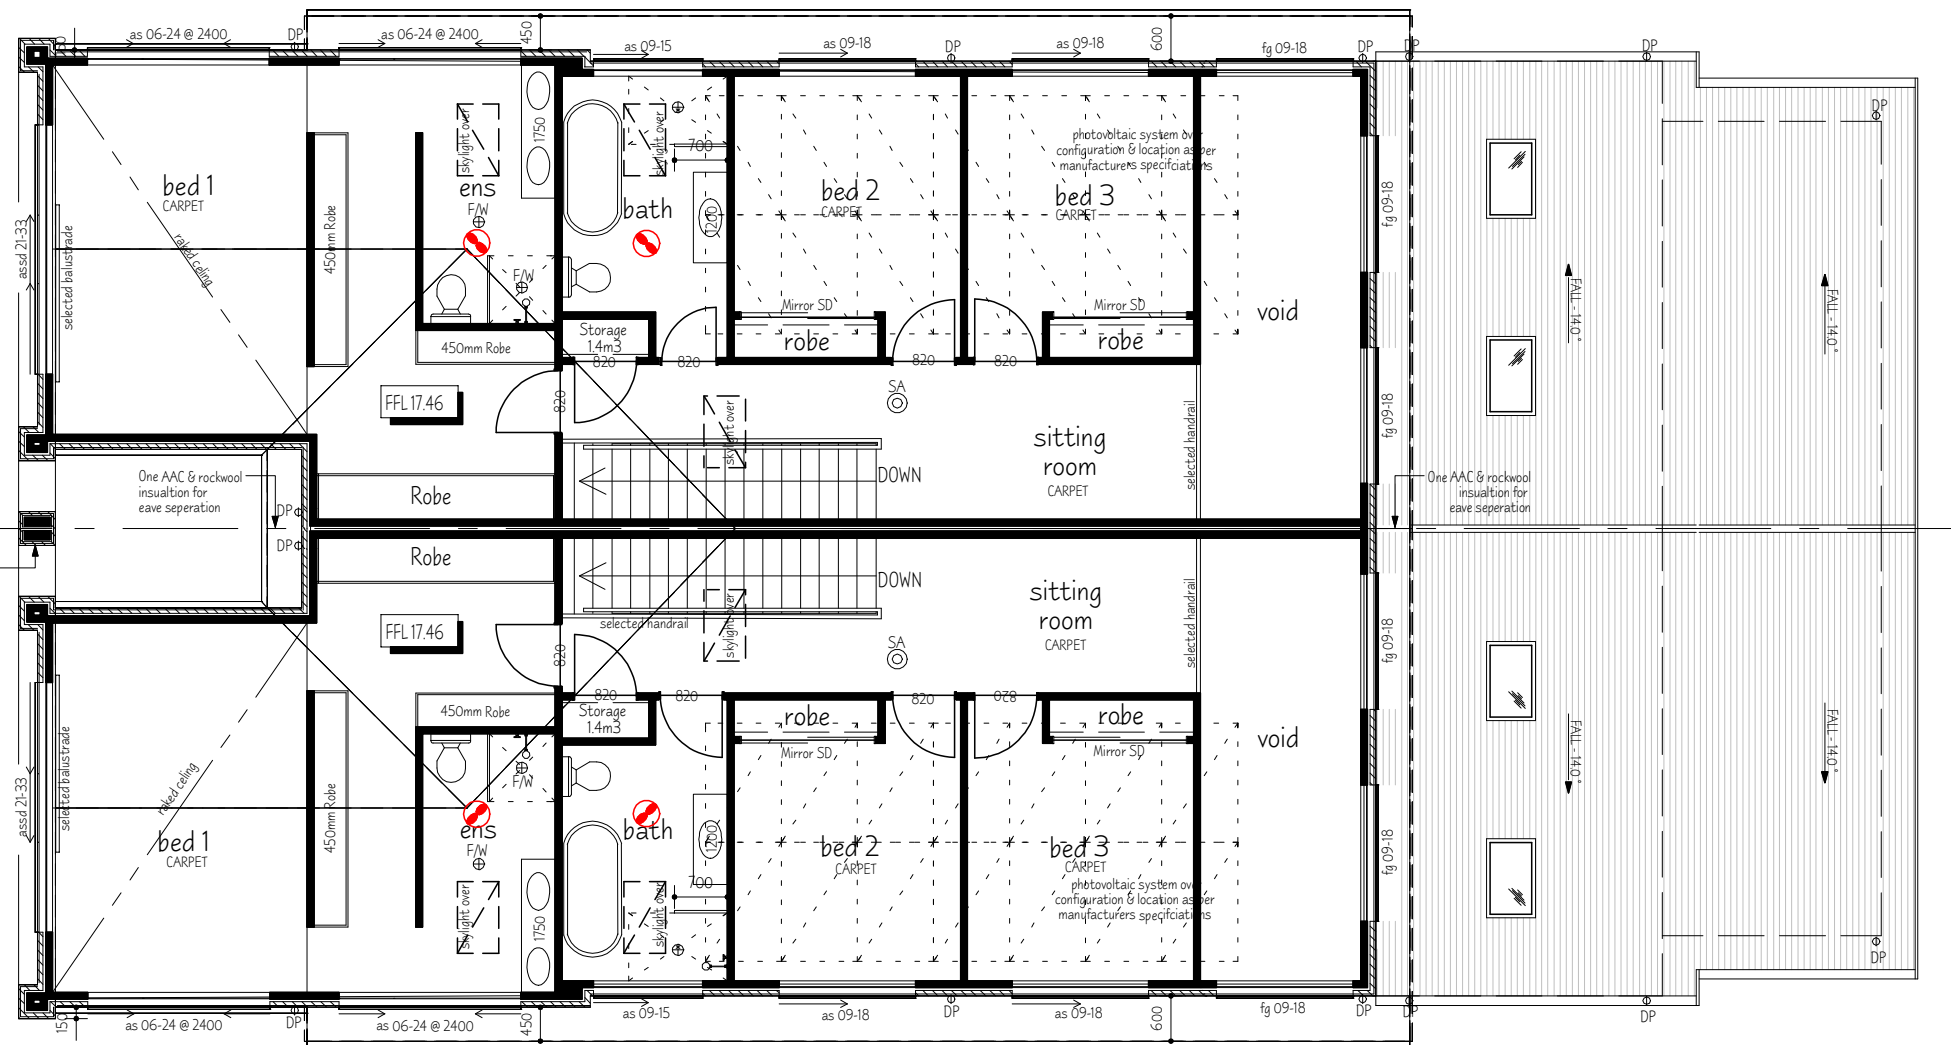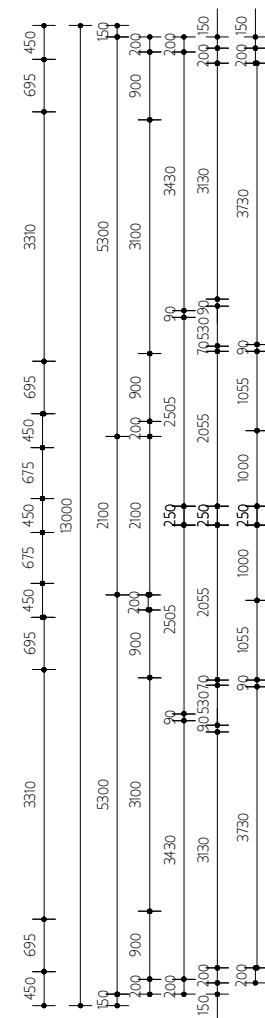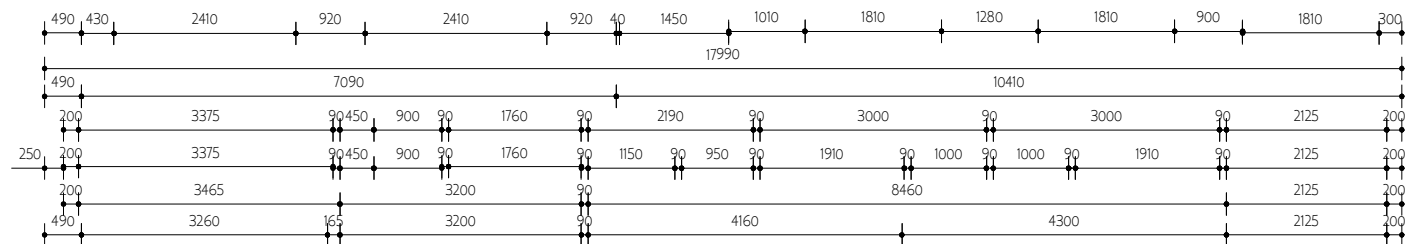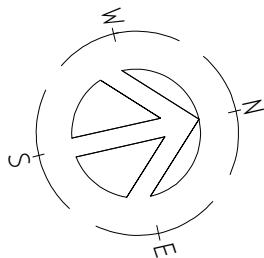

Itemised Floor Areas:	Totals:
ground floor:	198.0 m2
first floor	215.4 m2
garage:	45.2 m2
porch / balcony	7.2 m2
alfresco	31.4 m2
total floor area:	497.2 m2

FIRST FLOOR PLAN
scale 1:100

GENERAL NOTES
- Do not scale of the drawings unless otherwise stated as written dimensions will take preference over scaling
- All dimensions and levels are to be checked and verified by the CONTRACTOR on site before the commencement of any works, all dimensions and levels are subject to final survey and set-out. Discrepancies to be reported to the designer prior to commencement of any works
- Where Engineers drawings are required such must take preference over this set of drawings
- All work to be carried out in accordance with the Building Code of Australia, all Local and State Government Ordinances, relevant Australian Standards, Electricity and Water Authorities Regulations and all other relevant Authorities concerned.

All construction to be in
accordance with NCC
severe marine environment

ROOF TO BE VENTILATED AS PER
HOUSING PROVISIONS 10.8.3
CONDENSATION MANAGEMENT

VENTILATION TO BE AS PER
H4D9 PART 10.6 VENTILATION

MECHANICAL VENTILATION TO BE
DISCHARGED TO OUTSIDE AIR AS PER
H4D9 PART 10.8 - CONDENSATION MANAGEMENT
25 L/s FOR BATHROOMS
40 L/s FOR KITCHEN OR LAUNDRY

WATERPROOFING AS PER AS 3740.2021 &
HP 10.2 2022
WET AREA FALLS ARE TO BE IN
ACCORDANCE WITH HP 10.2.12 AND NCC H4D2

LOCATION OF NEW DOWNPIPES SHOWN
ARE SUBJECT TO VERIFICATION
BY THE BUILDER DURING CONSTRUCTION.
DOWNPIPES, SURFACE INLETS & KERB OUTLET
LOCATIONS MAY VARY PROVIDING COMPLIANCE
WITH AS/NZS 3500.3:2015 IS MAINTAINED.

VANITY SIZES SHOWN ARE APPROXIMATE
ONLY AND ARE TO BE CONFIRMED ON
SITE PRIOR TO INSTALLATION

- SHOWER RECESSES TO BE
350mm HIGH x 650mm WIDE
AT 1200mm ABOVE FFL

PROPOSED DUAL OCCUPANCY

client
AKABE HOLDINGS & ANTANGA

project
LOT 100 DP 15577
64 OAKS AVENUE
SHELLY BEACH

scale
1:100


drawn
J.S

date
17/06/26

drawing title
FLOOR PLANS

job no.
REW ---

issue
E.

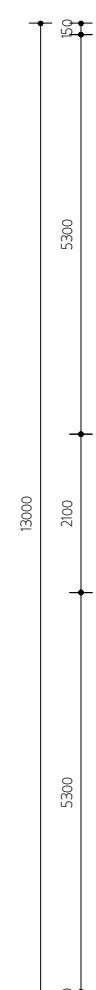

scale 1 : 100


Do not scale of the drawings unless otherwise stated as written dimensions will take preference over scaling

All dimensions and levels are to be checked and verified by the CONTRACTOR on the day before the commencement of any works, all dimensions and levels are subject to final survey and set-out. Discrepancies to be reported to the designer prior to commencement of any works


Where Engineers drawings are required such must take preference over this set of drawings

All work to be carried out in accordance with the Building Code of Australia, Electricity and Safety Regulations, the Australian Standards, the Australian Standards for Electricity and Water Authorities Regulations and all other relevant Authorities concerned.

drawing no.	issue
8/15	E.

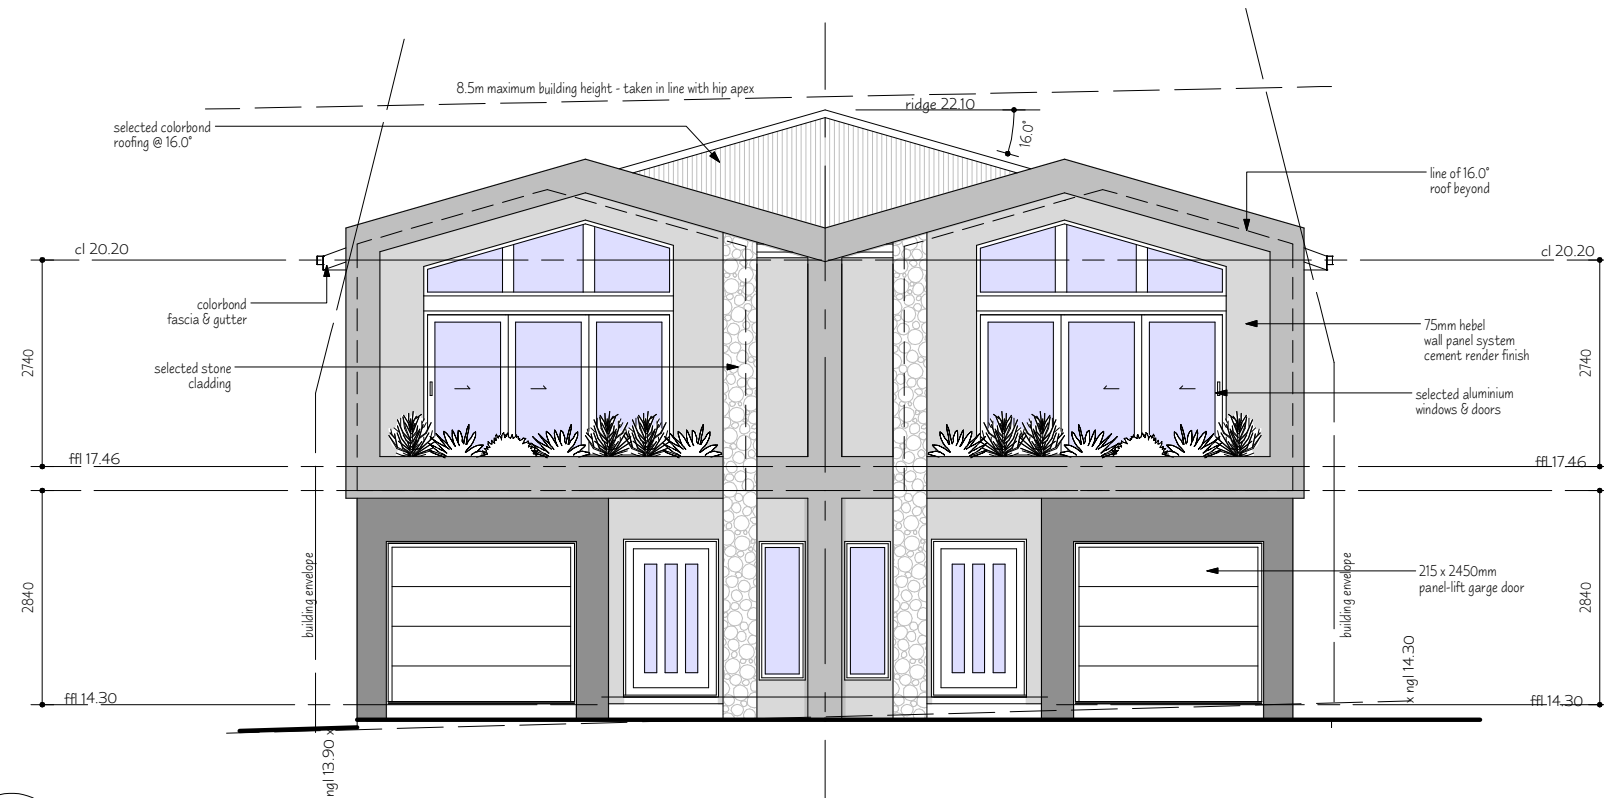

SOUTH ELEVATION
scale 1:100

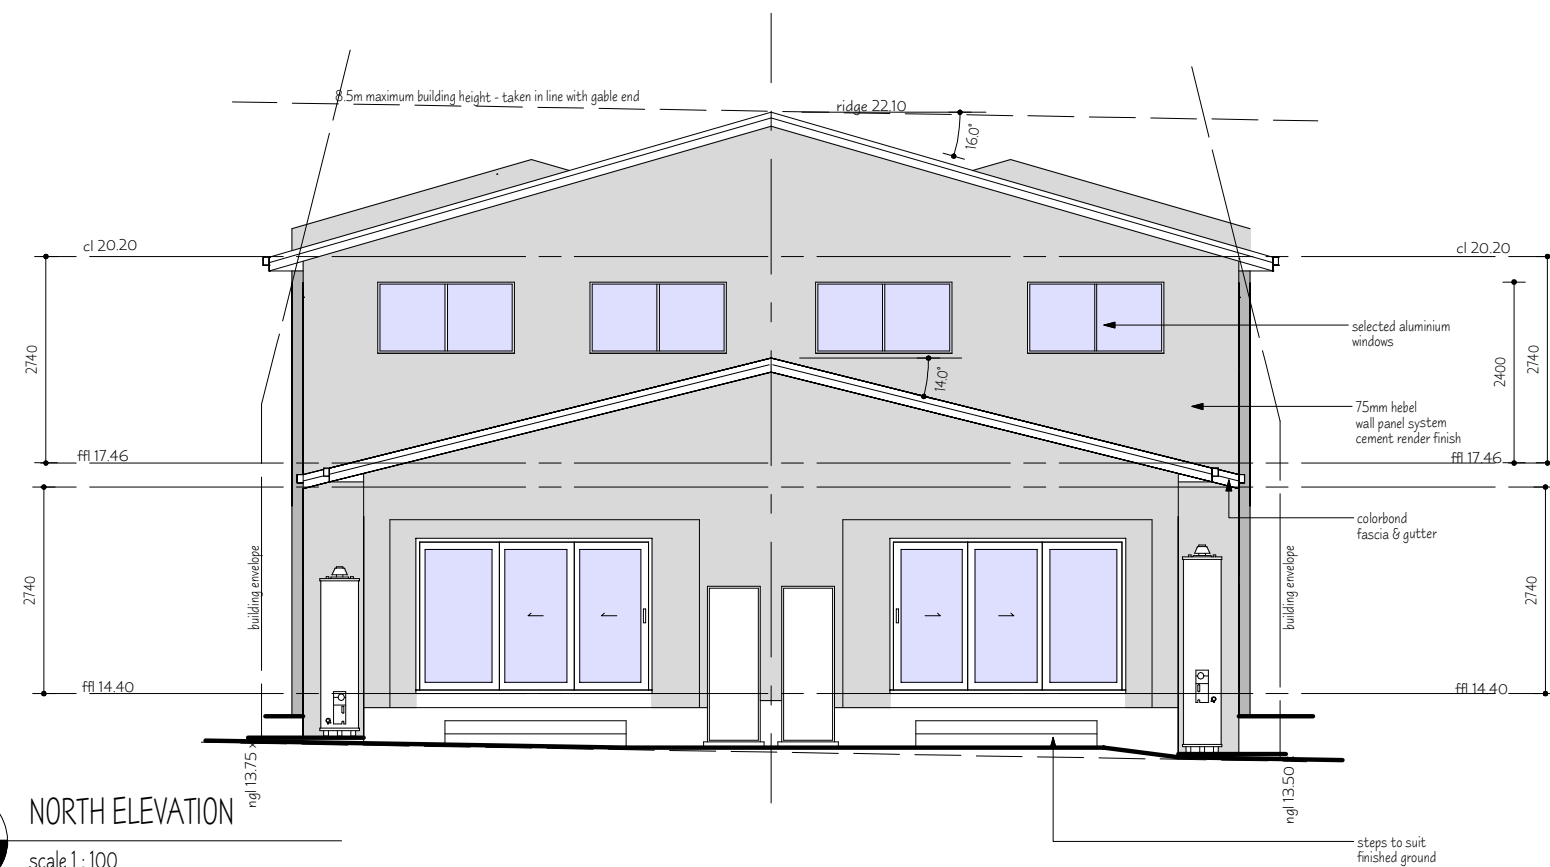

NORTH ELEVATION
scale 1:100

GENERAL NOTES

- Do not scale of the drawings unless otherwise stated as written dimensions will take preference over scaling
- All dimensions and levels are to be checked and verified by the CONTRACTOR on site before the commencement of any works, all dimensions and levels are subject to final survey and set-out. Discrepancies to be reported to the designer prior to commencement of any works
- Where Engineers drawings are required such must take preference over this set of drawings
- All work to be carried out in accordance with the Building Code of Australia, all Local and State Government Ordinances, relevant Australian Standards, Electricity and Water Authorities Regulations and all other relevant Authorities concerned.

PROPOSED DUAL OCCUPANCY

client
AKABE HOLDINGS & ANTANGA

project
**LOT 100 DP 15577
64 OAKS AVENUE
SHELLY BEACH**

scale
1:100

drawn
J.S


date
17/06/26

drawing title
ELEVATIONS


job no.
REW ---

drawing no.
9/15

issue
E.

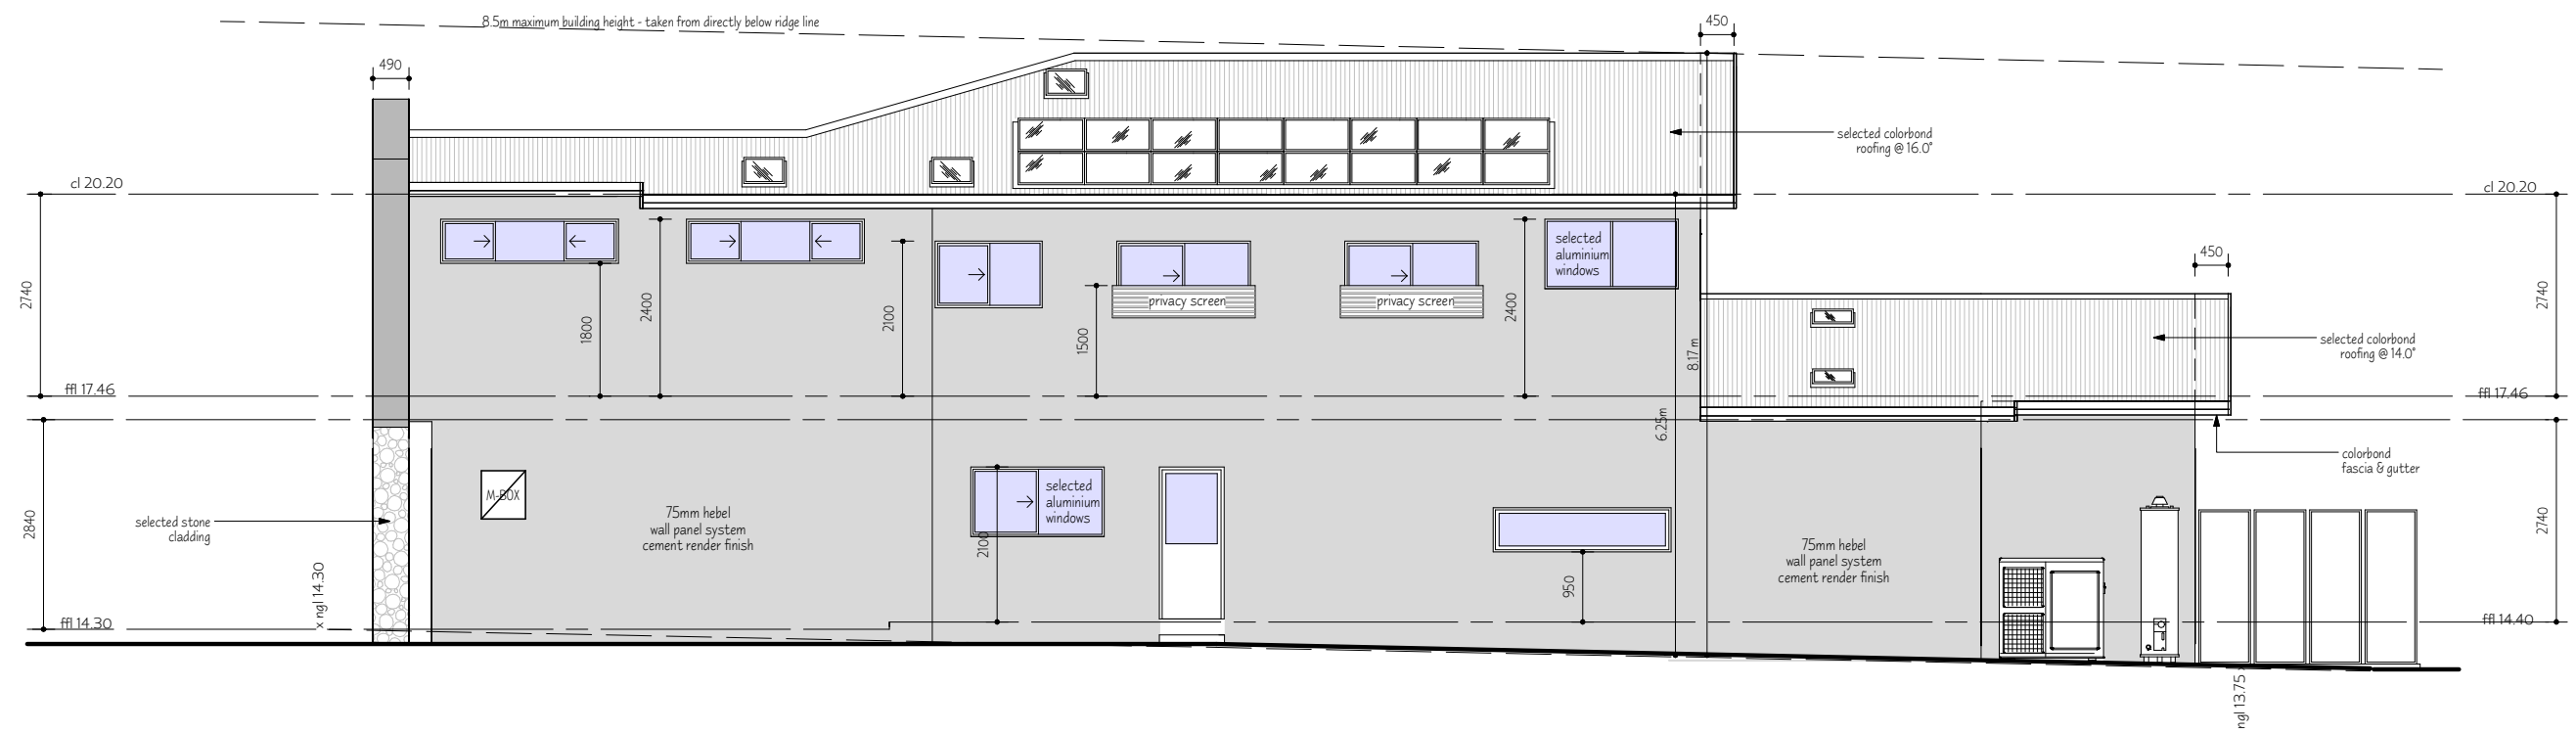

EAST ELEVATION
scale 1:100

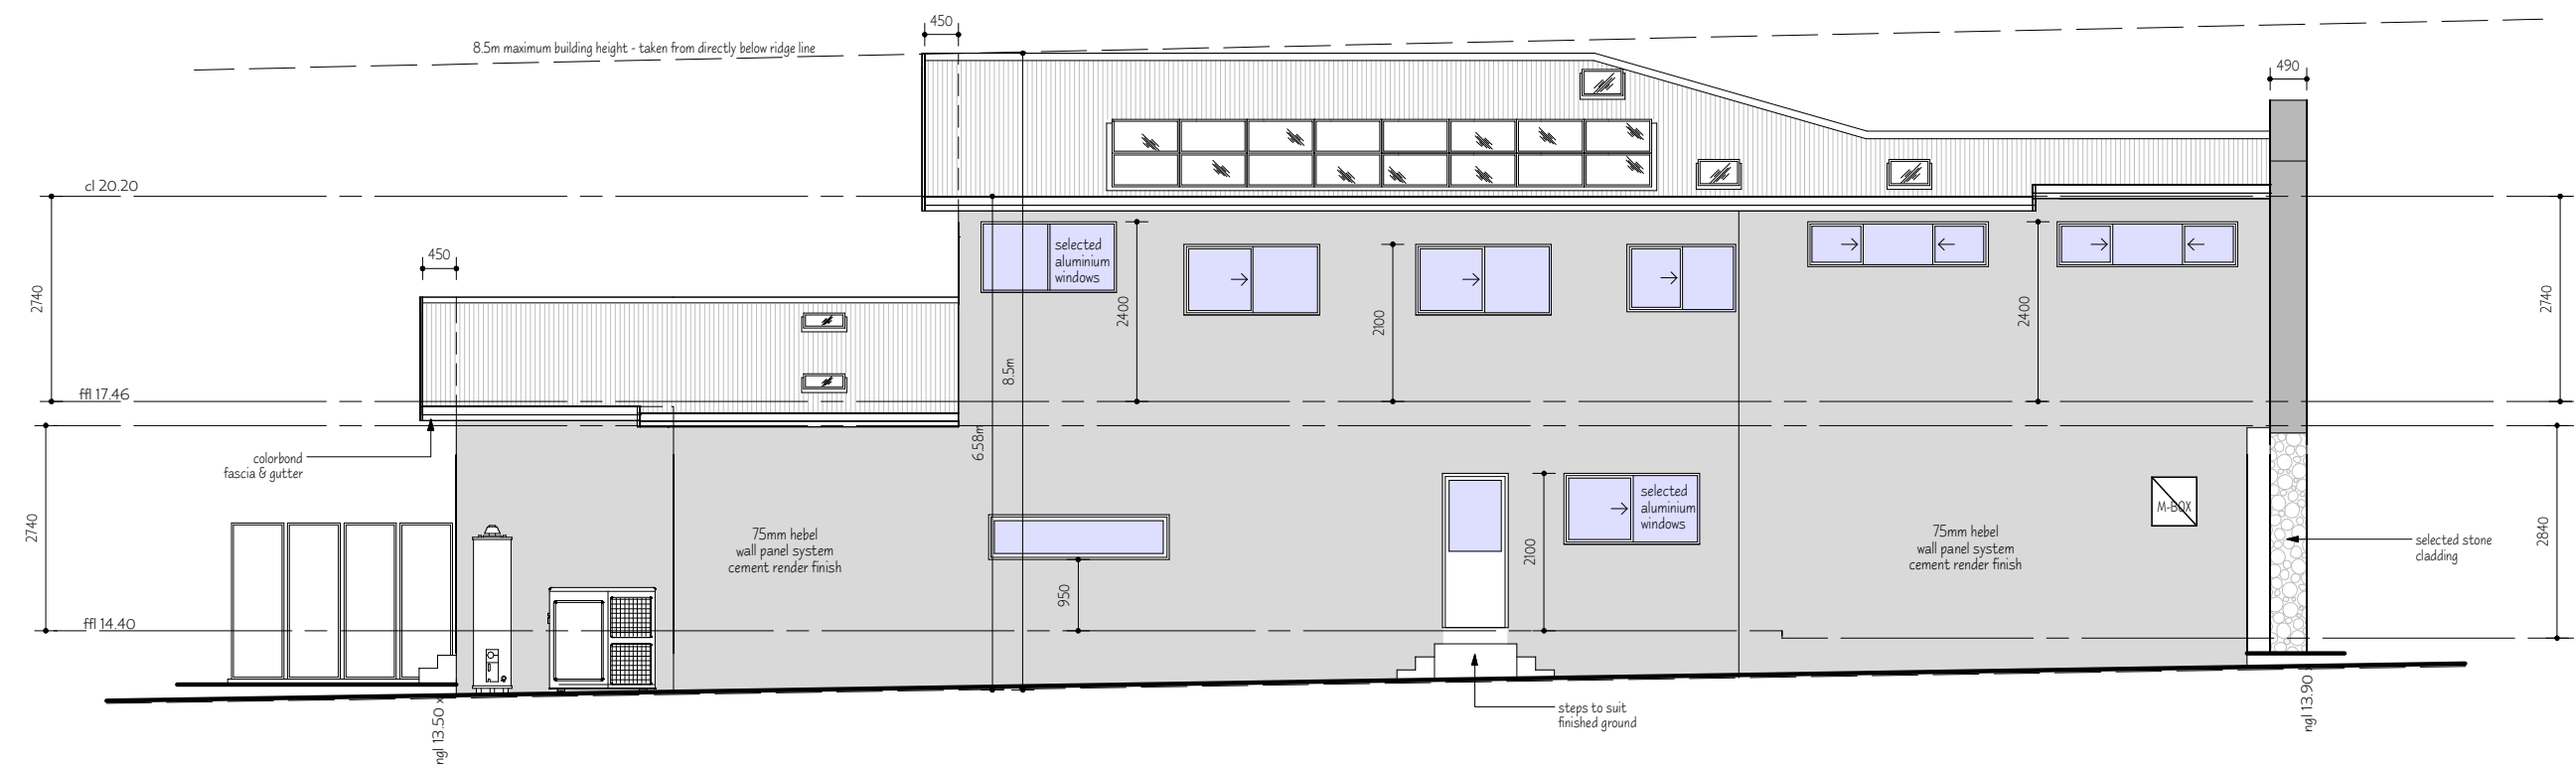

WEST ELEVATION
scale 1:100

GENERAL NOTES

- Do not scale of the drawings unless otherwise stated as written dimensions will take preference over scaling
- All dimensions and levels are to be checked and verified by the CONTRACTOR on site before the commencement of any works, all dimensions and levels are subject to final survey and set-out. Discrepancies to be reported to the designer prior to commencement of any works.
- Where Engineers drawings are required such must take preference over this set of drawings
- All work to be carried out in accordance with the Building Code of Australia, all Local and State Government Ordinances, relevant Australian Standards, Electricity and Water Authorities Regulations and all other relevant Authorities concerned.


PROPOSED DUAL OCCUPANCY

client
AKABE HOLDINGS & ANTANGA

project
**LOT 100 DP 15577
64 OAKS AVENUE
SHELLY BEACH**

scale	1:100	drawing title ELEVATIONS	
drawn	J.S	job no. REW ---	
date	17/06/26	drawing no. 10/15	issue E.

PROTECTION OF FIRST FLOOR OPENABLE WINDOWS
- AS PER BCA CLAUSE 3.9.2.5
- SLIDING WINDOWS TO HAVE A LOCKING OPTION
AT A MAXIMUM OPENING OF 125mm
- AWNING WINDOWS WINDERS RESTRICTED TO 125mm

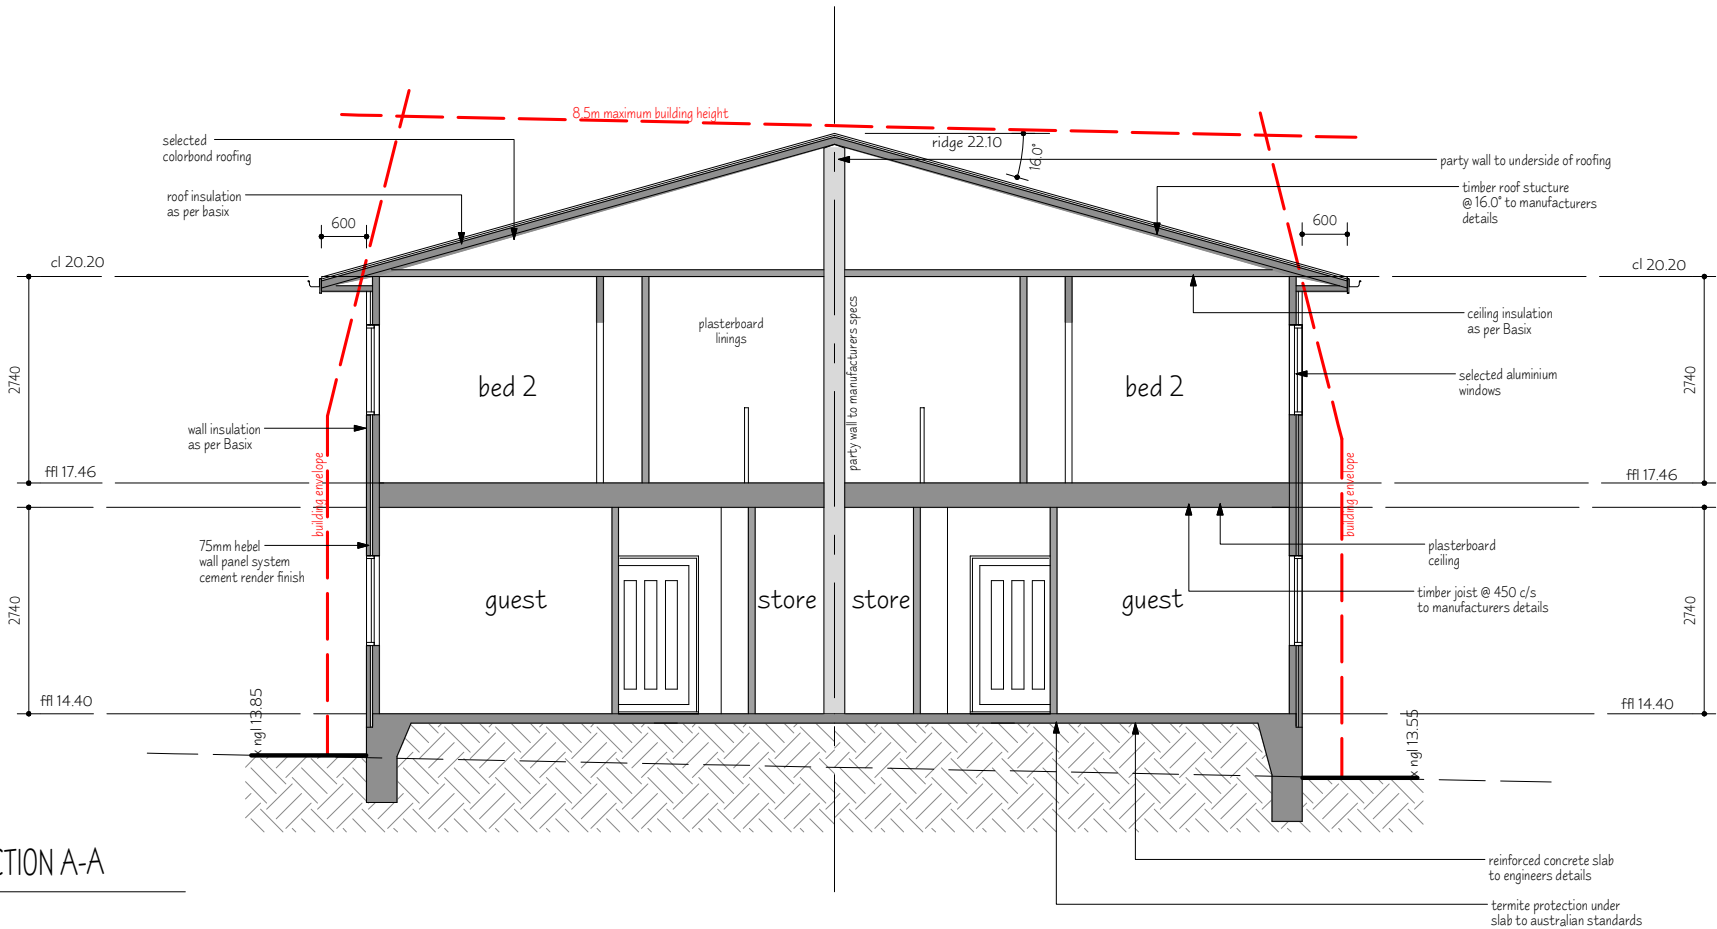

GENERAL NOTES
- Do not scale of the drawings unless otherwise stated as written dimensions will take preference over scaling
- All dimensions and levels are to be checked and verified by the CONTRACTOR on site before the commencement of any works, all dimensions and levels are subject to final survey and set-out. Discrepancies to be reported to the designer prior to commencement of any works
- Where Engineers drawings are required such must take preference over this set of drawings
- All work to be carried out in accordance with the Building Code of Australia, all Local and State Government Ordinances, relevant Australian Standards, Electricity and Water Authorities Regulations and all other relevant Authorities.

All construction to be in accordance with NCC severe marine environment

Window No.	Room	Code	Dimension	Type	Basix	U-Value	SHGC
Lot 1001							
1	entry	aa 18-06	1800 x 610	awning	BRD-112-005	5.2	0.53 - 0.58
2	guest	as 09-18	900 x 1810	sliding	BRD-001-021	4.6	0.64 - 0.70
3	kitchen	fg 06-24	600 x 2410	fixed	BRD-063-016	4.1	0.63 - 0.69
4	family	assd 21-32	2100 x 3215	stacker door	BRD-141-021	2.8	0.48 - 0.53
5	bed 1	assd 21-33	210 0x 3300	stacker door	BRD-141-021	2.8	0.48 - 0.53
6	bed 1	as 06-24	600 x 2410	sliding	BRD-001-037	6.4	0.70 - 0.78
7	ensuite	as 06-24	600 x 2410	sliding	BRD-001-037	6.4	0.70 - 0.78
8	bath	as 09-15	900 x 1450	sliding	BRD-001-037	6.4	0.70 - 0.78
9	bed 2	as 09-18	900 x 1810	sliding	BRD-001-021	4.6	0.64 - 0.70
10	bed 3	as 09-18	900 x 1810	sliding	BRD-001-021	4.6	0.64 - 0.70
11	void	fg 09-18	90 0x 1810	fixed	BRD-074-010	2.8	0.58 - 0.64
12	void	fg 09-18	900 x 1810	fixed	BRD-074-010	2.8	0.58 - 0.64
13	void	fg 09-18	900 x 1810	fixed	BRD-074-010	2.8	0.58 - 0.64
14	rake	n/a	3300 x 1000	fixed	BRD-074-010	2.8	0.58 - 0.64

WINDOW SCHEDULES TO BE READ IN CONJUNCTION WITH SELECTED PLANS, ELEVATIONS, BASIX AND NATHERS CERTIFICATES AND NOT TO BE RELIED ON SOLELY FOR QUOTING AND CONSTRUCTION PURPOSES

DIMENSIONS MAY VARY DEPENDING ON WINDOW MANUFACTURER AND ARE TO BE CONFIRMED BY BUILDER AND WINDDOW MANUFACTURER PRIOR TO ANY QUOTING, ORDERING OR CONSTRUCTION.

Window No.	Room	Code	Dimension	Type	Basix	U-Value	SHGC
Lot 1002							
1	entry	aa 18-06	1800 x 610	awning	BRD-112-005	5.2	0.53 - 0.58
2	guest	as 09-18	900 x 1810	sliding	BRD-001-021	4.6	0.64 - 0.70
3	kitchen	fg 06-24	600 x 2410	fixed	BRD-063-016	4.1	0.63 - 0.69
4	family	assd 21-32	2100 x 3215	stacker door	BRD-141-021	2.8	0.48 - 0.53
5	bed 1	assd 21-33	210 0x 3300	stacker door	BRD-141-021	2.8	0.48 - 0.53
6	bed 1	as 06-24	600 x 2410	sliding	BRD-001-037	6.4	0.70 - 0.78
7	ensuite	as 06-24	600 x 2410	sliding	BRD-001-037	6.4	0.70 - 0.78
8	bath	as 09-15	900 x 1450	sliding	BRD-001-037	6.4	0.70 - 0.78
9	bed 2	as 09-18	900 x 1810	sliding	BRD-001-021	4.6	0.64 - 0.70
10	bed 3	as 09-18	900 x 1810	sliding	BRD-001-021	4.6	0.64 - 0.70
11	void	fg 09-18	90 0x 1810	fixed	BRD-074-010	2.8	0.58 - 0.64
12	void	fg 09-18	900 x 1810	fixed	BRD-074-010	2.8	0.58 - 0.64
13	void	fg 09-18	900 x 1810	fixed	BRD-074-010	2.8	0.58 - 0.64
14	rake	n/a	3300 x 1000	fixed	BRD-074-010	2.8	0.58 - 0.64

WINDOW SCHEDULES TO BE READ IN CONJUNCTION WITH SELECTED PLANS, ELEVATIONS, BASIX AND NATHERS CERTIFICATES AND NOT TO BE RELIED ON SOLELY FOR QUOTING AND CONSTRUCTION PURPOSES

DIMENSIONS MAY VARY DEPENDING ON WINDOW MANUFACTURER AND ARE TO BE CONFIRMED BY BUILDER AND WINDDOW MANUFACTURER PRIOR TO ANY QUOTING, ORDERING OR CONSTRUCTION.

PROPOSED DUAL OCCUPANCY

client
AKABE HOLDINGS & ANTANGA


project
LOT 100 DP 15577
64 OAKS AVENUE
SHELLY BEACH

scale
1:100
drawing title
SECTION

drawn
J.S
job no.
REW ---

date
17/06/26
drawing no.
11/15
issue
E.

SYSTEM 1 – 60 MINUTE OPTION

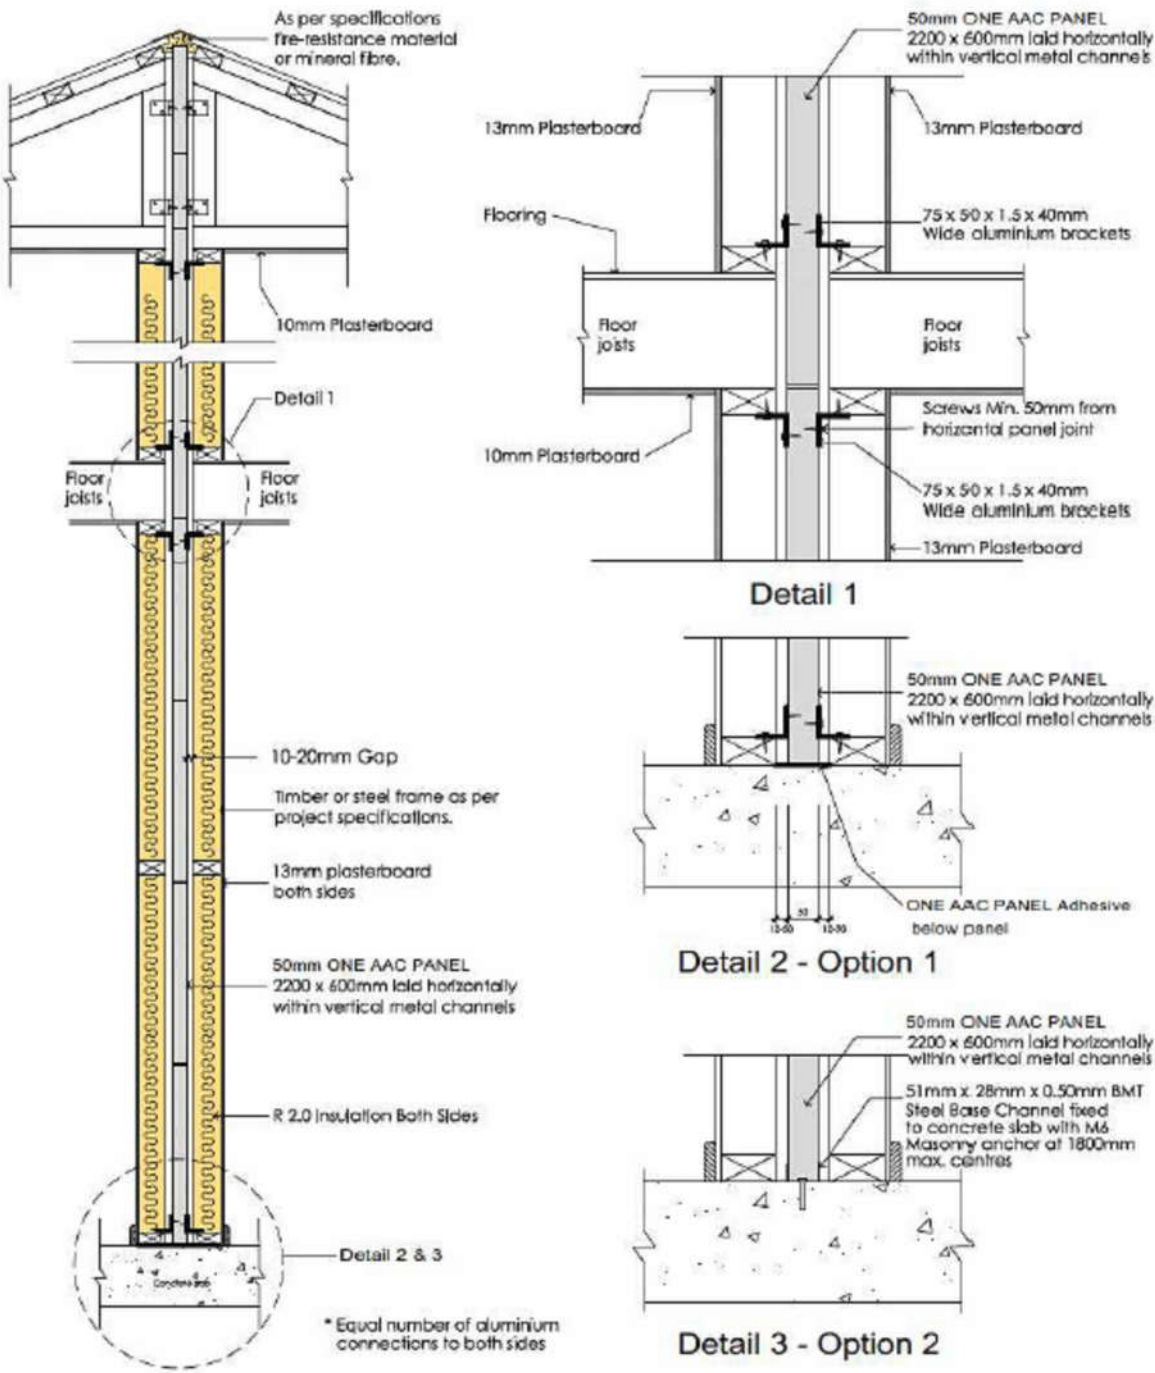

ONE AAC PANEL - PARTY WALL DETAIL - SYSTEM 2
FRL 60/60/60 Rw+Ctr 53

PARTY WALL DETAIL

Climate Zone 5 Condensation Requirements

10.8.1 External wall construction

- (1) Where a pliable building membrane is installed in an external wall, it must—
- A) comply with AS 4200.1; and
 - B) be installed in accordance with AS 4200.2; and
 - C) be located on the exterior side of the primary insulation layer of wall assemblies that form the external envelope of a building.
- (2) Where a pliable building membrane, sarking-type material or insulation layer is installed on the exterior side of the primary insulation layer of an external wall it must have a vapour permeance of not less than—
- A) in climate zones 4 and 5, 0.143 µg/N.s; and
 - B) in climate zones 6, 7 and 8, 1.14 µg/N.s.
- (3) Except for single skin masonry or single skin concrete, where a pliable building membrane is not installed in an external wall, the primary water control layer must be separated from water sensitive materials by a drained cavity.

10.8. Exhaust systems

- (1) An exhaust system installed in a kitchen, bathroom, sanitary compartment or laundry must have a minimum flow rate of —
- A) 25 L/s for a bathroom or sanitary compartment; and
 - B) 40 L/s for a kitchen or laundry.
- (2) Exhaust from a kitchen, kitchen range hood, bathroom, sanitary compartment or laundry must discharge directly or via a shaft or duct to outdoor air.
- (3) Where a venting clothes dryer is installed, it must discharge directly or via a shaft or duct to outdoor air.
- (4) An exhaust system that is not run continuously and is serving a bathroom or sanitary compartment that is not ventilated in accordance with 10.6.2(a) must—
- A) be interlocked with the room's light switch; and
 - B) include a run-on timer so that the exhaust system continues to operate for 10 minutes after the light switch is turned off.
- (5) Except for rooms that are ventilated in accordance with 10.6.2(a), a room with an exhaust system in accordance with (1) must be provided with make-up air—
- A) via openings to an adjacent room with a free area of 14,000 mm²; or
 - B) in accordance with AS 1668.2.
- (6) Except for rooms that are ventilated in accordance with 10.6.2(a), a room with an exhaust system in accordance with (3) must be provided with make-up air in accordance with AS 1668.2.

CLIMATE ZONE 5 - CONDENSATION REQUIREMENTS

GENERAL NOTES
- Do not scale of the drawings unless otherwise stated as written dimensions will take preference over scaling
- All dimensions and levels are to be checked and verified by the CONTRACTOR on site before the commencement of any works, all dimensions and levels are subject to final survey and set-out. Discrepancies to be reported to the designer prior to commencement of any works.
- Where Engineers drawings are required such must take preference over this set of drawings
- All work to be carried out in accordance with the Building Code of Australia, all Local and State Government Ordinances, relevant Australian Standards, Electricity and Water Authorities Regulations and all other relevant Authorities concerned.

PROPOSED DUAL OCCUPANCY

scale N/A

drawing title DETAILS

client AKABE HOLDINGS & ANTANGA

drawn J.S

job no. REW ---

project LOT 100 DP 15577
64 OAKS AVENUE
SHELLY BEACH

date 17/06/26

drawing no. 12/15

issue E.



Loxo cavity battens (continuous)

Timber or steel structural frame

Wall wrap (if required)

Damp proof course (DPC).

Concrete slab

Back block where required.

Loxo approved Coating System

Alkali fibreglass mesh.

Loxo cavity battens (segmented)

Loxo 50mm AAC panel system in a stretcher-bond pattern.

ONE AAC PANEL

FRYS ENERGY WISE				BASIX & THERMAL COMMITMENTS				New Homes & Apartments Renovations Swimming Pools Childcare Centres Commercial & Industrial Building				
Date: 21/05/22		Job Number: 64 Oaks Ave Shelly Beach		Version: 2		REQUIRED CHANGES HIGHLIGHTED						
Unit/Number	Lot	DP	Street	Suburb			Post Code			State		
64	100	15577	Oaks Ave	Shelly Beach						NSW		
Floors												
Material		Added Insulation			To Cantilever/Suspended			Floor Coverings				
Ground	Waffle Pod 225mm							As shown on plans				
1st Floor	Timber	R2.0 Insulation			Between Levels Throughout			R2.0 Insulation				
Walls												
Colour		External Material		Insulation		Internal Material		Internal Insulated				
Ground	Default	ACC Hebel Timber Frame		R2.0, Non Reflective Wrap		Plaster Timber 70mm		L'dry		R2.0		
1st Floor	Default	ACC Hebel Timber Frame		R2.0, Non Reflective Wrap		Plaster Timber 70mm		Bath		R2.0		
Common Internal Walls		Shaft Liner System		R2.0 both sides				Garage		R2.0		
Ceilings												
Material		Insulation to Roof Above			Roof		Insulation		Material		Colour	
Ground	Plaster Timber Frame	R5.0 R2.5 to Low Edge			Ground		Anticon 50mm (R1.3)		Metal		Default	
1st Floor	Plaster Timber Frame	R5.0 R2.5 to Low Edge			1st Floor		Anticon 50mm (R1.3)		Metal		Default	
Glazing												
Please Refer to the NATHERS (or BASIX) Certificate for all external glazing. To comply you must use glazing with the same opening and frame type, the U value must be the same or lower and have an SHGC value within the range given, THE BELOW GLAZING NOMINATIONS ARE AN INDICATION ONLY PLEASE REFERENCE THE CERTIFICATE(S).												
Supplier		Glazing Type Required		Location(s) of Glazing Required								
Bradnam's		Standard Single Clear		All Wet Areas								
		Low-e Single Clear		Throughout excluding wet areas								
		Low-e Double Glaze		Voids, Bed 1 and Family ASSD 21-32								
		Skylights		Family, Void, Hallway, Bath and Ens								
Notes												
Ceiling Fans												
Location		Fan Size										
Water												
Landscape Area		Low Water Area		Rain Water Tank, connected to,			Roof Area to Tank		Recycled Water, connected to,			
296.8 m2		m2		2,000L ea. Garden, WC, Laundry			80% of Roof		No			
Showerheads				Toilets		Kitchen Taps		Bathroom Taps		Swimming Pool		
3 Star > 7.5 but less < or = 9.0 litres per minute				4 Star		4 Star		4 Star		No		
Energy												
Hot Water		Rating		Air Conditioning					Other			
Electric Storage		.		Cooling 3.0 - 3.5 EER - Heating 3.0 - 3.5 EER					Single Phase			
Solar Photovoltaic System		Orientation 1		Orientation 2		Cooking						
Yes		West		1.5 KW		East		1.5 KW		Electric Cooktop/ Electric Oven		
Ventilation												
Laundry		Bathroom		Kitchen								
Ducted		Ducted		Ducted								
Notes												
Bed 1 raked ceiling												
- Multi dwelling certificate - Green AAC wall / 25mm battens / wall wrap to external walls - Energy STAR to a minimum - Ray Gaps - Solar photovoltaic system												

GENERAL NOTES

- Do not scale of the drawings unless otherwise stated as written dimensions will take preference over scaling
- All dimensions and levels are to be checked and verified by the CONTRACTOR on site before the commencement of any works, all dimensions and levels are subject to final survey and set-out. Discrepancies to be reported to the designer prior to commencement of any works
- Where Engineers drawings are required such must take preference over this set of drawings
- All work to be carried out in accordance with the Building Code of Australia, all Local and State Government Ordinances, relevant Australian Standards, Electricity and Water Authorities Regulations and all other relevant Authorities concerned.

PROPOSED DUAL OCCUPANCY		scale N/A		drawing title DETAILS	
client AKABE HOLDINGS & ANTANGA		drawn J.S		job no. REW ---	
project LOT 100 DP 15577 64 OAKS AVENUE SHELLY BEACH		date 17/06/26	drawing no. 13/15		issue E.

BASIX™ Certificate

Building Sustainability Index
www.planningportal.nsw.gov.au/development-and-assessment/basix

Multi Dwelling

Certificate number: 1796453M_02

This certificate confirms that the proposed development will meet the NSW government's requirements for sustainability, if it is built in accordance with the commitments set out below. Terms used in this certificate, or in the commitments, have the meaning given by the document entitled "BASIX Definitions" dated 10/09/2020 published by the Department. This document is available at www.planningportal.nsw.gov.au/definitions

Secretary
Date of issue: Thursday, 06 November 2025
To be valid, this certificate must be submitted with a development application or lodged with a complying development certificate application within 3 months of the date of issue.



When submitting this BASIX certificate with a development application or complying development certificate application, it must be accompanied by NatHERS certificate 0011935350.

Project summary		
Project name	64 Oaks Ave Shelly Beach_02	
Street address	64 OAKS AVENUE SHELLY BEACH 2261	
Local Government Area	CENTRAL COAST	
Plan type and plan number	Deposited Plan 15577	
Lot No.	100	
Section no.	-	
No. of residential flat buildings	0	
Residential flat buildings: no. of dwellings	0	
Multi-dwelling housing: no. of dwellings	2	
No. of single dwelling houses	0	
Project score		
Water	✔ 45	Target 40
Thermal Performance	✔ Pass	Target Pass
Energy	✔ 70	Target 70
Materials	✔ -90	Target n/a

Common area landscape	
Common area lawn (m²)	0
Common area garden (m²)	0
Area of indigenous or low water use species (m²)	0
Assessor details and thermal loads	
Assessor number	DMN/12/1441
Certificate number	0011935350
Climate zone	15
Project score	
Water	✔ 45 Target 40
Thermal Performance	✔ Pass Target Pass
Energy	✔ 70 Target 70
Materials	✔ -90 Target n/a

Project address	
Project name	64 Oaks Ave Shelly Beach
Street address	64 OAKS AVENUE SHELLY BEACH 2261
Local Government Area	CENTRAL COAST
Plan type and plan number	Deposited Plan 15577
Lot No.	100
Section no.	-
Project type	
No. of residential flat buildings	0
Residential flat buildings: no. of dwellings	0
Multi-dwelling housing: no. of dwellings	2
No. of single dwelling houses	0
Site details	
Site area (m²)	695.5
Roof area (m²)	320.4
Non-residential floor area (m²)	0
Residential car spaces	2
Non-residential car spaces	0

Multi-dwelling houses

Dwelling no.	No. of bedrooms	Conditioned floor area (m²)	Unconditioned floor area (m²)	Area of garden & lawn (m²)	Indigenous species (min area m²)
1001	4+	156.7	10.6	148.4	0

Dwelling no.	No. of bedrooms	Conditioned floor area (m²)	Unconditioned floor area (m²)	Area of garden & lawn (m²)	Indigenous species (min area m²)
1002	4+	156.7	10.6	148.4	0

	Fixtures					Appliances		Individual pool				Individual spa		
Dwelling no.	All shower-heads	All toilet flushing systems	All kitchen taps	All bathroom taps	HW recirculation or diversion	All clothes washers	All dish-washers	Volume (max volume)	Pool cover	Pool location	Pool shaded	Volume (max volume)	Spa cover	Spa shaded
All dwellings	3 star (> 7.5 but <= 9 L/min)	4 star	4 star	4 star	-	-	-	-	-	-	-	-	-	-

	Alternative water source								
Dwelling no.	Alternative water supply systems	Size	Configuration	Landscape connection	Toilet connection (s)	Laundry connection	Pool top-up	Spa top-up	
All dwellings	Individual water tank (No. 1)	Tank size (min) 2000 liters	To collect run-off from at least: 128 square metres of roof area;	yes	yes	yes	no	no	

	Hot water	Bathroom ventilation system		Kitchen ventilation system		Laundry ventilation system	
Dwelling no.	Hot water system	Each bathroom	Operation control	Each kitchen	Operation control	Each laundry	Operation control
All dwellings	electric storage	individual fan, ducted to façade or roof	manual switch on/off	individual fan, ducted to façade or roof	manual switch on/off	individual fan, ducted to façade or roof	manual switch on/off

	Cooling		Heating		Natural lighting	
Dwelling no.	living areas	bedroom areas	living areas	bedroom areas	No. of bathrooms or toilets	Main Kitchen
All dwellings	1-phase airconditioning - ducted / EER 3.0 - 3.5	1-phase airconditioning - ducted / EER 3.0 - 3.5	1-phase airconditioning - ducted / EER 3.0 - 3.5	1-phase airconditioning - ducted / EER 3.0 - 3.5	2	yes

	Individual pool			Individual spa		Appliances other efficiency measures				
Dwelling no.	Pool heating system	Pool Pump	Timer	Spa heating system	Timer	Kitchen cooktop/oven	Dishwasher	Clothes dryer	Indoor or sheltered clothes drying line	Private outdoor or unsheltered clothes drying line
All dwellings	-	-	-	-	-	electric cooktop & electric oven	-	-	no	yes

	Alternative energy		
Dwelling no.	Photovoltaic system (min rated electrical output in peak kW)	Photovoltaic collector installation	Orientation inputs
1001	between >10° to <=25° degree to the horizontal	1.5	E
All other dwellings	between >10° to <=25° degree to the horizontal	1.5	W

	Thermal loads		
Dwelling no.	Area adjusted heating load (in MJ/m²/yr)	Area adjusted cooling load (in MJ/m²/yr)	Area adjusted total load (in MJ/m²/yr)
1001	29.3	20.2	49.500
All other dwellings	31.2	19.6	50.800

GENERAL NOTES
- Do not scale of the drawings unless otherwise stated as written dimensions will take preference over scaling
- All dimensions and levels are to be checked and verified by the CONTRACTOR on site before the commencement of any works, all dimensions and levels are subject to final survey and set-out. Discrepancies to be reported to the designer prior to commencement of any works.
- Where Engineers drawings are required such must take preference over this set of drawings
- All work to be carried out in accordance with the Building Code of Australia, all Local and State Government Ordinances, relevant Australian Standards, Electricity and Water Authorities Regulations and all other relevant Authorities concerned.

PROPOSED DUAL OCCUPANCY
client
AKABE HOLDINGS & ANTANGA
project
LOT 100 DP 15577
64 OAKS AVENUE
SHELLY BEACH

scale
N/A
drawing title
BASIX
drawn
J.S
job no.
REW ---
date
17/06/26
drawing no.
14/15
issue
E.

		Construction of floors and walls								
Dwelling no.	Concrete slab on ground (m²)		Suspended floor with open subfloor (m²)		Suspended floor with enclosed subfloor (m²)		Suspended floor above garage (m²)		Primarily rammed earth or mudbrick walls	
All dwellings	92.4		9.3		-		19.6		no	

Floor types										
	Concrete slab on ground				Suspended floor above enclosed subfloor			Suspended floor above open subfloor		
Dwelling no.	Area (m²)	Insulation	Low emissions option	Dematerialisation	Construction type	Area (m²)	Insulation	Construction type	Area (m²)	Insulation
All dwellings	92.4	-	-	waffle pod slab	-	-	-	particle board, frame: timber - H2 treated softwood	9.3	-

Floor types											
	First floor above habitable rooms or mezzanine			Suspended floor above garage			Garage floor				
Dwelling no.	Construction type	Area (m²)	Insulation	Construction type	Area (m²)	Insulation	Construction type	Area (m²)	Insulation	Low emissions option	Dematerialisation
All dwellings	particle board, frame: timber - H2 treated softwood	46	-	particle board, frame: timber - H2 treated softwood	19.6	-	concrete slab on ground	16.2	-	-	waffle pod slab

External walls									
	External wall type 1					External wall type 2			
Dwelling no.	Wall type	Area (m²)	Insulation	Low emissions option	Wall type	Area (m²)	Insulation	Low emissions option	
All dwellings	AAC veneer, frame : timber - H2 treated softwood	118.5	-	-	-	-	-	-	

Internal walls									
	Internal walls shared with garage			Internal wall type 1			Internal wall type 2		
Dwelling no.	Wall type	Area (m²)	Insulation	Wall type	Area (m²)	Insulation	Wall type	Area (m²)	Insulation
All dwellings	plasterboard, frame: timber - H2 treated softwood	17.2	-	plasterboard, frame: timber - H2 treated softwood	89.7	-	plasterboard, frame: timber - H2 treated softwood	43.2	-

Ceiling and roof									
	Flat ceiling / pitched roof			Raked ceiling / pitched or skillion roof			Flat ceiling / flat roof		
Dwelling no.	Construction type	Area (m²)	Insulation	Construction type	Area (m²)	Insulation	Construction type	Area (m²)	Insulation
All dwellings	framed - metal roof, frame: timber - H2 treated softwood	160.2	Ceiling:fibreglass batts or roll, Roof: foil backed blanket	-	-	Ceiling:,Roof:	-	-	Ceiling:,Roof:

Glazing type										Frame types				
Dwelling no.	Single glazing (m²)	Double glazing (m²)	Triple glazing (m²)	Aluminium frames (m²)	Timber frames (m²)	uPVC frames (m²)	Steel frames (m²)	Composite frames (m²)						
All dwellings	10.4	22.3	-	32.7	-	-	-	-						

GENERAL NOTES

- Do not scale of the drawings unless otherwise stated as written dimensions will take preference over scaling
- All dimensions and levels are to be checked and verified by the CONTRACTOR on site before the commencement of any works, all dimensions and levels are subject to final survey and set-out. Discrepancies to be reported to the designer prior to commencement of any works.
- Where Engineers drawings are required such must take preference over this set of drawings
- All work to be carried out in accordance with the Building Code of Australia, all Local and State Government Ordinances, relevant Australian Standards, Electricity and Water Authorities Regulations and all other relevant Authorities concerned.

Nationwide House Energy Rating Scheme®
Multiple Class 1 dwellings Summary
NatHERS® Certificate No. 0011935350

Generated on 21 May 2025 using BERS Pro v5.2.4 (3.23)

Property

Address 64 Oaks Avenue,
SHELLY BEACH , NSW , 2261
Lot/DP Lot 100 DP 15577
NatHERS Climate Zone 15 Williamtown



Accredited assessor

Name Ian Fry
Business name Frys Energywise
Email comply@frysenergywise.com.au
Phone 02 9899 2825
Accreditation No. DMN/12/1441
Assessor Accrediting Organisation Design Matters National

Verification

To verify this certificate, scan the QR code or visit hstar.com.au/QR/Generate?p=XRyZvMqg. When using either link, ensure you are visiting hstar.com.au



National Construction Code (NCC) requirements

The NCC allows the use of NatHERS accredited software to comply with the energy efficiency requirements for houses (Class 1 buildings) and apartments (Class 2 sole-occupancy units and Class 4 parts of buildings). The applicable requirements for houses are detailed in Specification 42 of NCC Volume Two. For apartments the requirements are detailed in clauses J3D3 and J3D15 of NCC Volume One.

NCC 2022 includes enhanced thermal performance requirements for houses and apartments. It also includes a new whole-of-home annual energy use budget which applies to the major equipment in the home.

The NCC, and associated ABCB Standards and support material, can be accessed at www.abcb.gov.au.

Note, variations and additions to the NCC energy efficiency requirements may apply in some states and territories.

Summary of all dwellings

Certificate number and link	Unit Number	Heating load (load limit) [MJ/m²/p.a.]	Cooling load (load limit) [MJ/m²/p.a.]	Total load [MJ/m²/p.a.]	Star Rating	Whole of Home Rating
0011935335	1001	29.3 (N/A)	20.2 (N/A)	49.5	7.1	0
0011935327	1002	31.2 (N/A)	19.6 (N/A)	50.9	7	0

PROPOSED DUAL OCCUPANCY

client
AKABE HOLDINGS & ANTANGA

project
LOT 100 DP 15577
64 OAKS AVENUE
SHELLY BEACH

scale
N/A

drawn
J.S

date
17/06/26

drawing title
BASIX

job no.
REW ---

drawing no.
15/15

issue
E.