

Proposed Dwelling House

DHIMAN STREET, CLAREMONT MEADOWS

LOT 117

Drawings list

DA.000	Cover Page
DA.001	Site Analysis Plan
DA.100	Site Plan
DA.101	Cut & Fill Plan
DA.201	Ground Floor Plan
DA.202	First Floor Plan
DA.203	Roof Plan
DA.300	Elevations
DA.301	Elevations
DA.303	Sections/Window Schedule
DA.400	Concept Landscape Plan
DA.500	Concept Stromwater Plan
DA.501	Erosion and Sendimentation Conrtrol
DA.600	Shadow Diagram
DA.601	Shadow Diagram
DA.602	Shadow Diagram
DA.603	Shadow Diagram
DA.604	Shadow Diagram
DA.605	Shadow Diagram
DA.606	Shadow Diagram
DA.700	Finishes Schedule

BUILDING SPECIFICATIONS
National Construction Code - Volume 2 -
Building Code of Australia 2022 & Housing Provisions Standard 2022
SITE PREPARATION
- PART 3.1 OF THE NCC VOLUME 2 BUILDING CODE OF AUSTRALIA 2022 & HOUSING PROVISIONS STANDARD 2022.

EARTHWORKS
- TO BE CARRIED OUT IN ACCORDANCE WITH THE REQUIREMENTS OF THE ENVIRONMENTAL PLANNING & ASSESSMENT ACT 1979 AND DEVELOPMENT CONSENT CONDITIONS
- PART 3.2 OF THE NCC VOLUME 2 BUILDING CODE OF AUSTRALIA 2022 & HOUSING PROVISIONS STANDARD 2022.
- AS 4678:2002 - EARTH-RETAINING STRUCTURES

DRAINAGE
- PART 3.3 OF THE NCC VOLUME 2 BUILDING CODE OF AUSTRALIA 2022 & HOUSING PROVISIONS STANDARD 2022.
- AS/NZS 3500.1:2021 - PLUMBING & DRAINAGE - WATER SERVICES
- AS/NZS 3500.2:2021 - PLUMBING & DRAINAGE - SANITARY PLUMBING & DRAINAGE
- AS/NZS 3500.3:2021 - PLUMBING & DRAINAGE STORMWATER DRAINAGE
- AS/NZS 3500.4:2021 - PLUMBING & DRAINAGE - HEATED WATER SERVICES

STRUCTURAL WORK
- Part 2.2 OF THE NCC VOLUME 2 BUILDING CODE OF AUSTRALIA 2022 & HOUSING PROVISIONS STANDARD 2022.
- AS 4100-2020- STEEL STRUCTURES CODES

- AS/NZS 1170.0-2002 - GENERAL PRINCIPLES
- ASNZS 1170.1-2002 - PARTS 1 PERMANENT, IMPOSED AND OTHER ACTIONS
- AS/NZS 1170.2-2021 - PART 2 WIND ACTIONS
- AS 3700-2018- SAA MASONRY CODE
- AS 1684.3-2021- RESIDENTIAL TIMBER FRAMED CONSTRUCTION

FOOTINGS & SLABS
- PART 4 OF THE NCC VOLUME 2 BUILDING CODE OF AUSTRALIA 2022 & HOUSING PROVISIONS STANDARD 2022.
- AS 2159:2009 - PILING - DESIGN & INSTALLATION

- AS 2870:2011 - RESIDENTIAL SLABS & FOOTINGS
- AS 3600:2018 - CONCRETE STRUCTURES **MASONRY**
- PART 5 OF THE NCC VOLUME 2 BUILDING CODE OF AUSTRALIA 2022 & HOUSING PROVISIONS STANDARD 2022.
- AS 3700:2018 - MASONRY STRUCTURES

FRAMING
- PART 6 OF THE NCC VOLUME 2 BUILDING CODE OF AUSTRALIA 2022 & HOUSING PROVISIONS STANDARD 2022.
- AS 1684.2:2021 - RESIDENTIAL TIMBER- FRAMED CONSTRUCTION - NON- CYCLONIC AREAS

- AS 1720.1:2010 - TIMBER STRUCTURES - DESIGN METHODS
- AS 4100:2020 - STEEL STRUCTURES
- AS 3660.1-2014 - TERMITE MANAGEMENT SYSTEM

ROOF & WALL CLADDING
- PART 7 OF THE NCC VOLUME 2 BUILDING CODE OF AUSTRALIA 2022 & HOUSING PROVISIONS STANDARD 2022.
- AS 1273:1991 - UNPLASTICIZED PVC (UPVC) DOWNPIPES & FITTINGS FOR RAINWATER
- AS 1562.1:2018 - DESIGN & INSTALLATION OF SHEET ROOF & WALL CLADDING - METAL

- AS/NZS 1562.2:1999 - DESIGN & INSTALLATION OF SHEET ROOF & WALL CLADDING - CORRUGATED FIBRE- REINFORCED CEMENT
- AS/NZS 1562.3:2006 - DESIGN & INSTALLATION OF SHEET ROOF & WALL CLADDING - PLASTIC
- AS 2049:2002 - ROOF TILES
- AS 2050:2018 - INSTALLATION OF ROOF TILES
- AS 4285:2019 - ROOFLIGHTS

GLAZING
- PART 8 OF THE NCC VOLUME 2 BUILDING CODE OF AUSTRALIA 2022 & HOUSING PROVISIONS STANDARD 2022.
- AS 1288:2021 - GLASS IN BUILDINGS - SELECTION & INSTALLATION

- AS 2047:2014 - WINDOWS & EXTERNAL GLAZED DOORS IN BUILDINGS
- AS/NZS 2208:1996 - SAFETY GLAZING MATERIALS IN BUILDINGS

FIRE SAFETY
- PART 9 OF THE NCC VOLUME 2 BUILDING CODE OF AUSTRALIA 2022 & HOUSING PROVISIONS STANDARD 2022.
- AS 3786:2014 - SMOKE ALARMS USING SCATTERED LIGHT, TRANSMITTED LIGHT OR IONIZATION

HEALTH & AMENITY
- PART 10 OF THE NCC VOLUME 2 BUILDING CODE OF AUSTRALIA 2022 & HOUSING PROVISIONS STANDARD 2022.

- AS/NZS ISO 717.1:2004 - ACOUSTICS - RATING OF SOUND INSULATION IN BUILDINGS & OF BUILDING ELEMENTS - AIRBORNE SOUND INSULATION
- AS ISO 717.2:2004 - ACOUSTICS - RATING OF SOUND INSULATION IN BUILDINGS & OF BUILDING ELEMENTS - IMPACT SOUND INSULATION

- AS 1668.2:2012 - THE USE OF VENTILATION & AIR CONDITIONING IN BUILDINGS - MECHANICAL VENTILATION IN BUILDINGS
- AS 1668.4:2012 - THE USE OF VENTILATION & AIR CONDITIONING IN BUILDINGS - NATURAL VENTILATION OF BUILDINGS
- AS/NZS 1680.0:2009 - INTERIOR LIGHTING
- SAFE MOVEMENT
- AS 3740:2021 - WATERPROOFING OF DOMESTIC WET AREAS
- AS 3000-2018 - ELECTRICAL INSTALLATION

WATERPROOFING
- AS 3740-2021- WATERPROOFING TO WET AREA
- AS 4654-2012 - EXTERNAL WET AREAS

SAFE MOVEMENT & ACCESS
- PART 11 OF THE NCC VOLUME 2 BUILDING CODE OF AUSTRALIA 2022 & HOUSING PROVISIONS STANDARD 2022.
- AS 1428.1:2009 - DESIGN FOR ACCESS & MOBILITY - GENERAL REQUIREMENTS FOR ACCESS - NEW BUILDING WORK
- AS 1657:2018 - FIXED PLATFORMS, WALKWAYS, STAIRWAYS & LADDERS - DESIGN, CONSTRUCTION & INSTALLATION

HANDRAILS & BALUSTRADE
- PART 11.3.3 OF THE NCC VOLUME 2 BUILDING CODE OF AUSTRALIA 2022 & HOUSING PROVISIONS STANDARD 2022.
- PART 11.3.4 OF THE NCC VOLUME 2 BUILDING CODE OF AUSTRALIA 2022 & HOUSING PROVISIONS STANDARD 2022.
- PART 11.3.5 OF THE NCC VOLUME 2 BUILDING CODE OF AUSTRALIA 2022 & HOUSING PROVISIONS STANDARD 2022.
- AS 1170.1-2002 - BALUSTRADE INSTALLATION

PROTECTION OF OPENABLE WINDOW
PART 11.3.7 AND 11.3.8 OF THE NCC VOLUME 2 BUILDING CODE OF AUSTRALIA 2022 & HOUSING PROVISIONS STANDARD 2022.
DEMOLITION
- AS 2601-2001 - DEMOLITION WORK

SWIMMING POOL
- PART 12.1.1 (H7D2) OF THE NCC VOLUME 2 BUILDING CODE OF AUSTRALIA 2022 & HOUSING PROVISIONS STANDARD 2022
- AS 1926 PART 1-2012 - SWIMMING POOL SAFETY- SAFETY BARRIERS FOR SWIMMING POOLS
- AS 1926 PART 2-2007 - SWIMMING POOL SAFETY- LOCATION OF SAFETY BARRIERS FOR SWIMMING POOLS (INCORPORATING AMENDMENTS 1 AND 2)
- AS 1926 PART 3-2010 - SWIMMING POOL SAFETY- WATER RECIRCULATION SYSTEMS (INCORPORATING AMENDMENT 1)

ENERGY EFFICIENCY
- PART 13 OF THE NCC VOLUME 2 BUILDING CODE OF AUSTRALIA 2022 & HOUSING PROVISIONS STANDARD 2022 & BASIX Certificate.

Site Area : 550.7m²
Max Ground Floor Area Allowed : 275.3m² (50% of Site Area)
Max Gross Floor Proposed : 249.3m² (45.2% of Site Area)
Max First Floor Area Allowed : 165.2m² (30% of Site Area)
Max Gross Floor Proposed : 223.3 m² (40.5% of Site Area)

Gross Area Table (Inc External Walls)		
	S.q.m	Square
ALFRESCO	23.3 m ²	2.5
BALCONY	13.0 m ²	1.4
FIRST FLOOR	220.0 m ²	23.7
GARAGE	42.3 m ²	4.6
GROUND FLOOR	207.2 m ²	22.3
PORCH	4.9 m ²	0.5
REAR BALCONY	23.3 m ²	2.5
VOID 1	7.4 m ²	0.8
VOID 2	21.6 m ²	2.3
	563.0 m ²	60.6

Landscape Area Required: =220.2 m²(40% of Site Area)
Total Landscape Provide = 249.7m² (45.3% of Site Area)

Private Open Space : 137.3m² - (PPOS min 24 m²)
Backyard space only

Summary of Key Controls with Lots with Frontage width > 15m for front accessed dwellings

ELEMENT	CONTROL
Front Setback (Min)	4.5m to building facade line; 3.5m to building facade fronting open space or drainage land. 3.0m to articulation zone; 2.0m to articulation zone fronting open space or drainage land. 5.5m to garage line and 1m behind the building line
Side setback (Min)	Ground Floor: 0.9m (Side A), 0.9m (Side B) Upper Floor: 0.9m (Side A), 1.5m (Side B)
Length of zero lot line on boundary	11m
Rear setback (min)	4m (ground level) and 6m (upper levels)
Corner lots secondary street setback (min)	2.0m
Building height, massing and siting	2 storeys maximum (3rd storey subject to clause 4.2.5 (1))
Site coverage	Single storey dwellings: 50% Two storey dwellings: Ground Floor 50% : Upper Floor 30%
Landscaped area	Minimum 30% of allotment area
Principal Private Open space (PPOS)	Minimum 24m ² with minimum dimension of 4.0m. 50% of the area of the required PPOS (of both the proposed development and adjoining properties) should receive at least 3 hours of sunlight between 9am and 3pm at the winter solstice (21 June)
Garages and car parking	Front or rear loaded double and tandem garages permitted Maximum garage door width 3m (Single) and 6m (Double) Triple garages are not permitted. 1-2 bedroom dwellings will provide at least 1 car space. 3 bedroom or more dwellings will provide at least 2 car spaces.



Job #MD1540 DA91



Disclaimer:

Do not sclae drawings, Work off figured dimensions.Verify all dimensions on site. Report any discrepancy to the designer.

Design and documentation there of are copyright and remain the property of Mistry Designs and must not be used in anyway, wholly or in part without the written consent of the designer

North

Drawing Title:

Cover Page

Sheet No:
DA.000

Lodged at:	Penrith Council	Scale
Drawn by	VT	Date 26JULY2025


PROJECT :

Proposed Dwelling House

Address:

DHIMAN STREET, CLAREMONT MEADOWS

C	Updated as per Council Requirements	NM	08.04.26
B	Updated as per Council Requirements	NM	22.03.26
A	Issue for DA	NM	25.11.25
Issue	Description	By	DATE

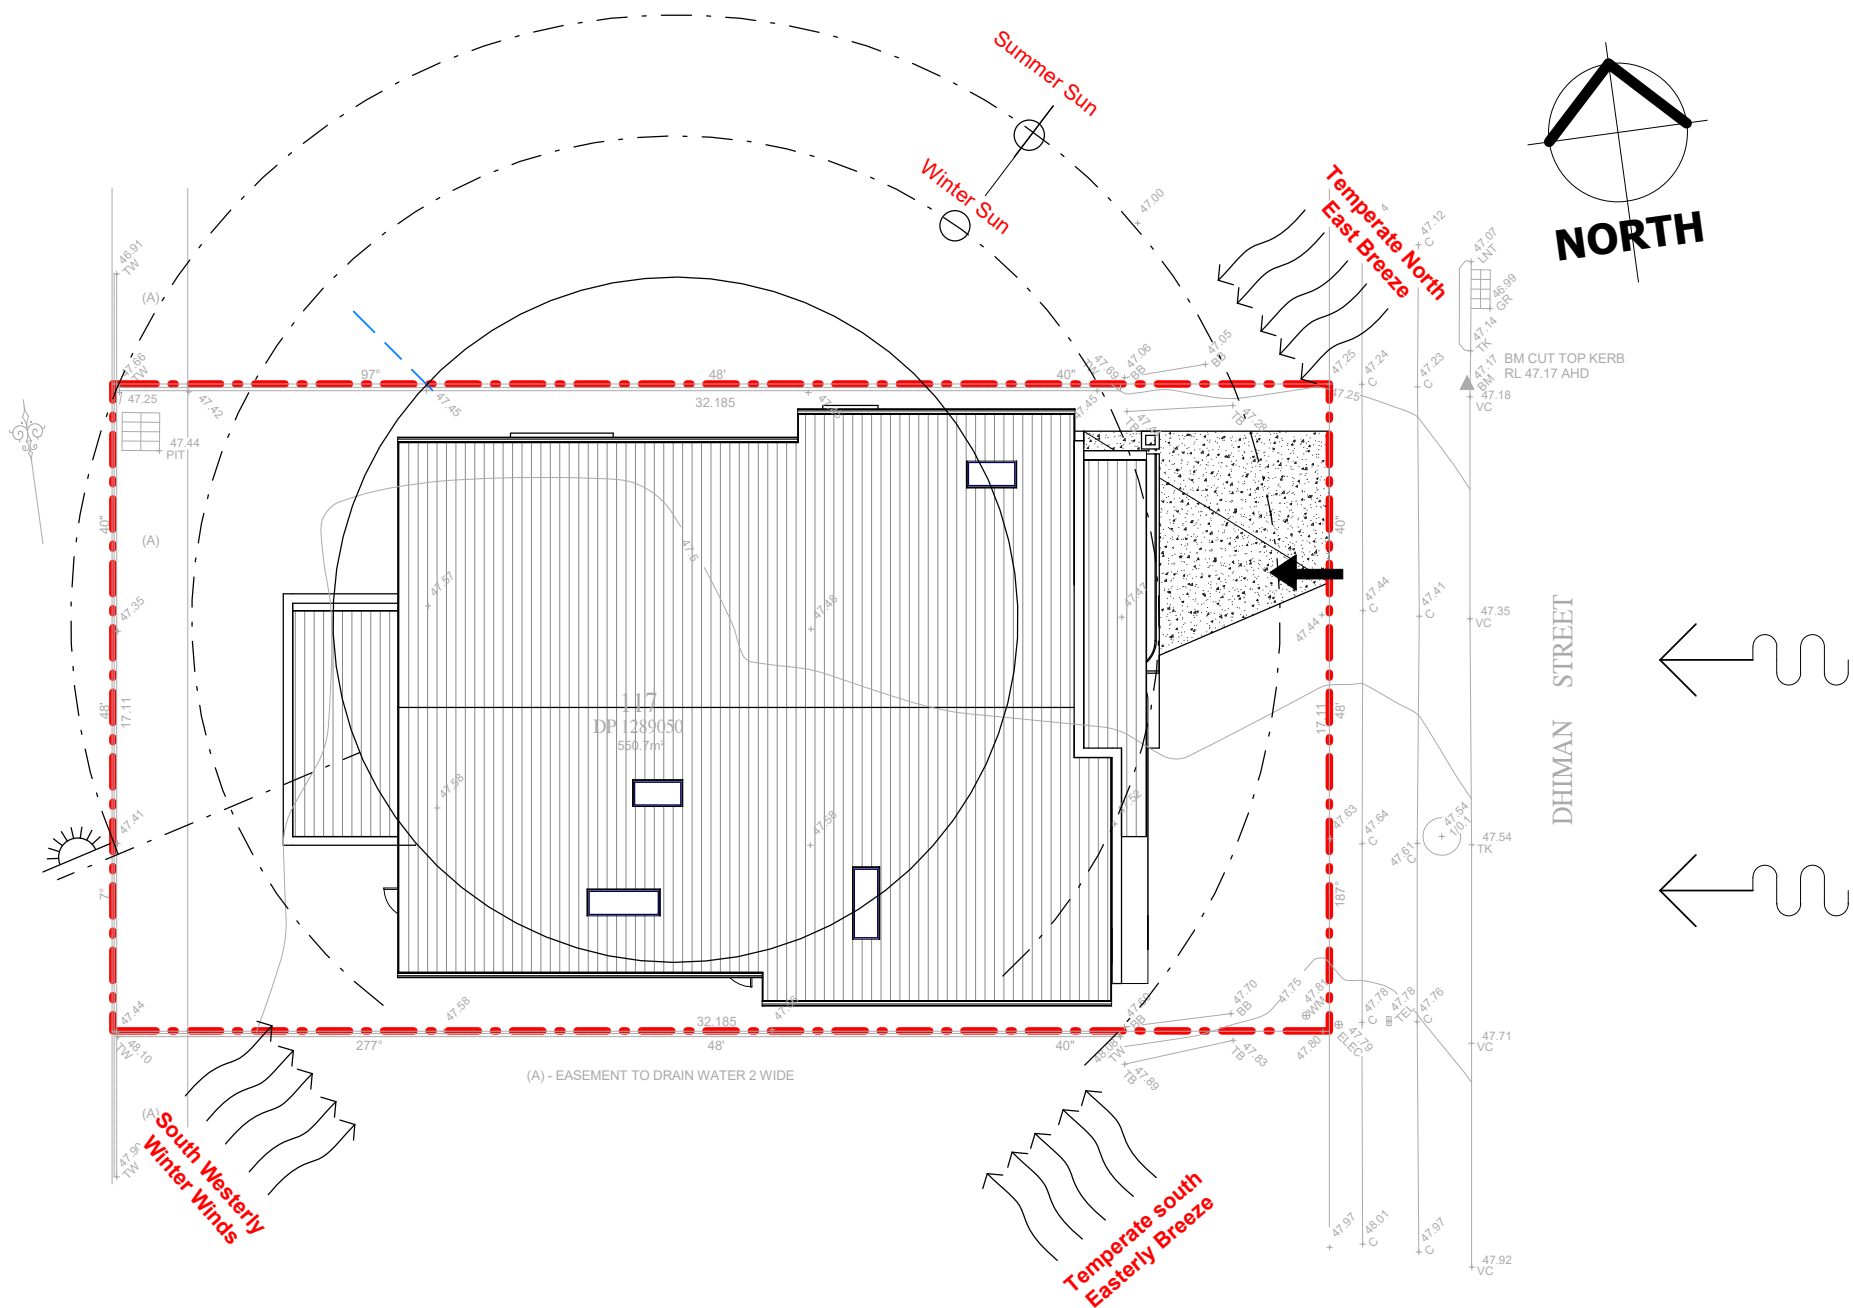

Site Analysis

1 : 200

Site Analysis Legend



**MISTRY
DESIGNS**

60 Weaver Street
Erskine Park, NSW 2759


m :0430657990
e :nish@nm3d.com.au



Disclaimer:

Do not scale drawings. Work off figured dimensions. Verify all dimensions on site. Report any discrepancy to the designer.

Design and documentation there of are copyright and remain the property of Mistry Designs and must not be used in anyway, wholly or in part without the written consent of the designer

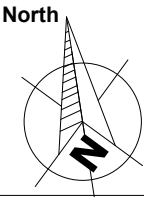

Drawing Title:

Site Analysis Plan

Sheet No:

DA.001

Lodged at:

Penrith Council

Scale

As indicated

Drawn by

VT

Date

26JULY2025

PROJECT :


Proposed Dwelling House

Address:

DHIMAN STREET, CLAREMONT MEADOWS
LOT 117



Job #MD1540 DA91

C	Updated as per Council Requirements	NM	08.04.26
B	Updated as per Council Requirements	NM	22.03.26
A	Issue for DA	NM	25.11.25
Issue	Description	By	DATE

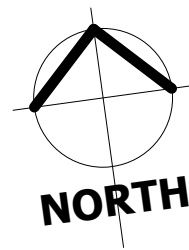

Site Plan

1 : 150

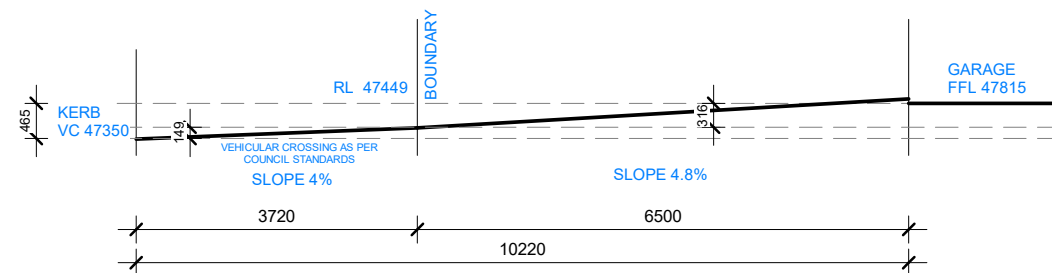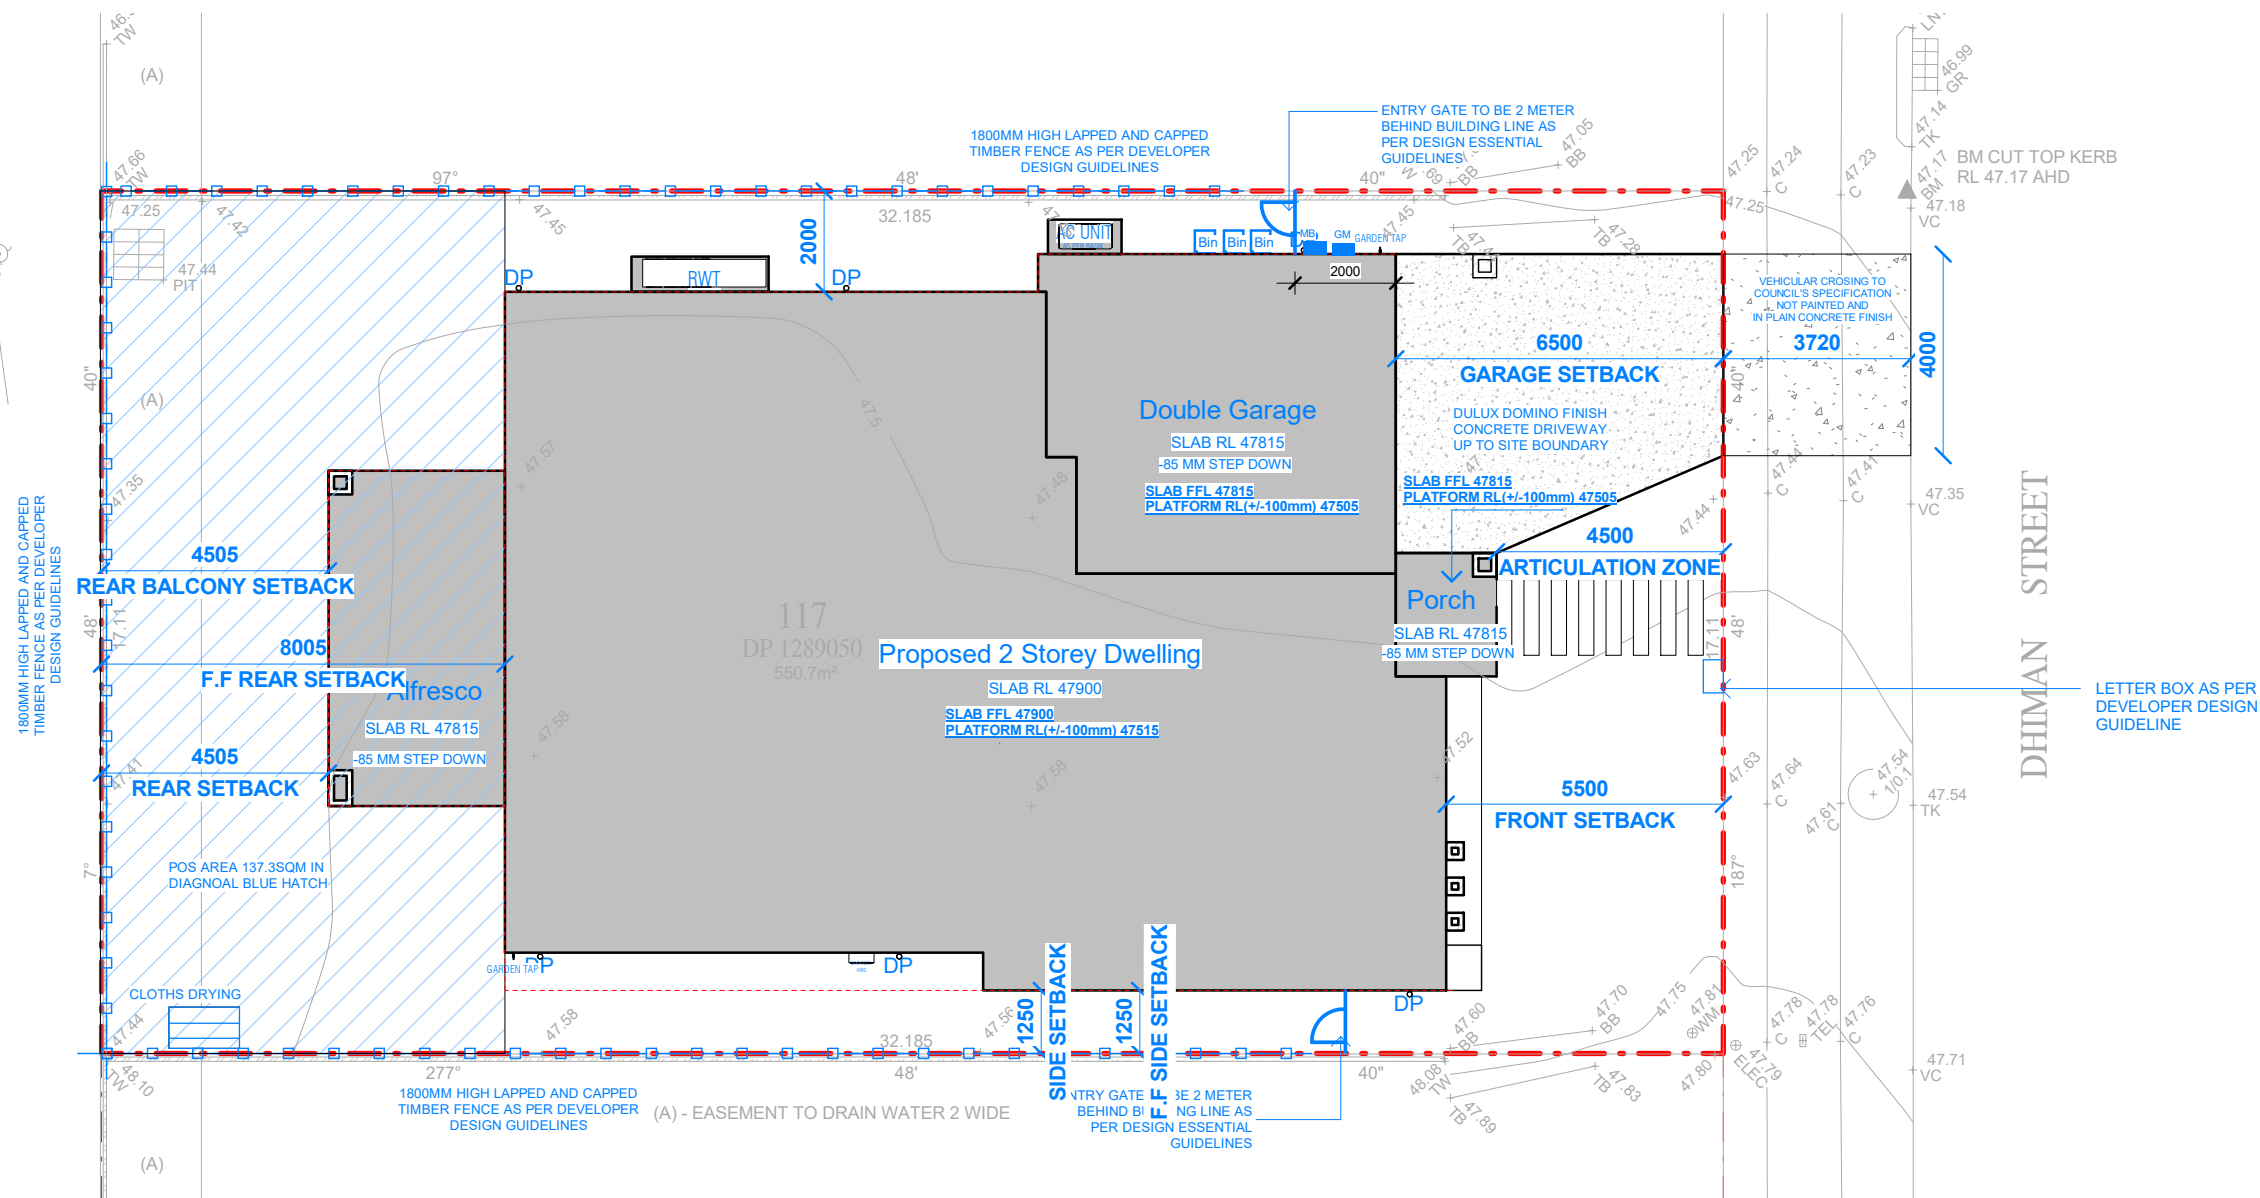

Driveway Section



**MISTRY
DESIGNS**

60 Weaver Street
Erskine Park, NSW 2759

m : 0430657990
e : nish@nm3d.com.au



Disclaimer:

Do not scale drawings. Work off figured dimensions. Verify all dimensions on site. Report any discrepancy to the designer.

Design and documentation there of are copyright and remain the property of Mistry Designs and must not be used in anyway, wholly or in part without the written consent of the designer



Drawing Title:

Site Plan

Sheet No:

DA.100

Lodged at:

Penrith Council

Scale

As indicated

Drawn by

VT

Date

26JULY2025

PROJECT :


Proposed Dwelling House

Address:

DHIMAN STREET, CLAREMONT MEADOWS
LOT 117

Job #MD1540 DA91

C	Updated as per Council Requirements	NM	08.04.26
B	Updated as per Council Requirements	NM	22.03.26
A	Issue for DA	NM	25.11.25
Issue	Description	By	DATE

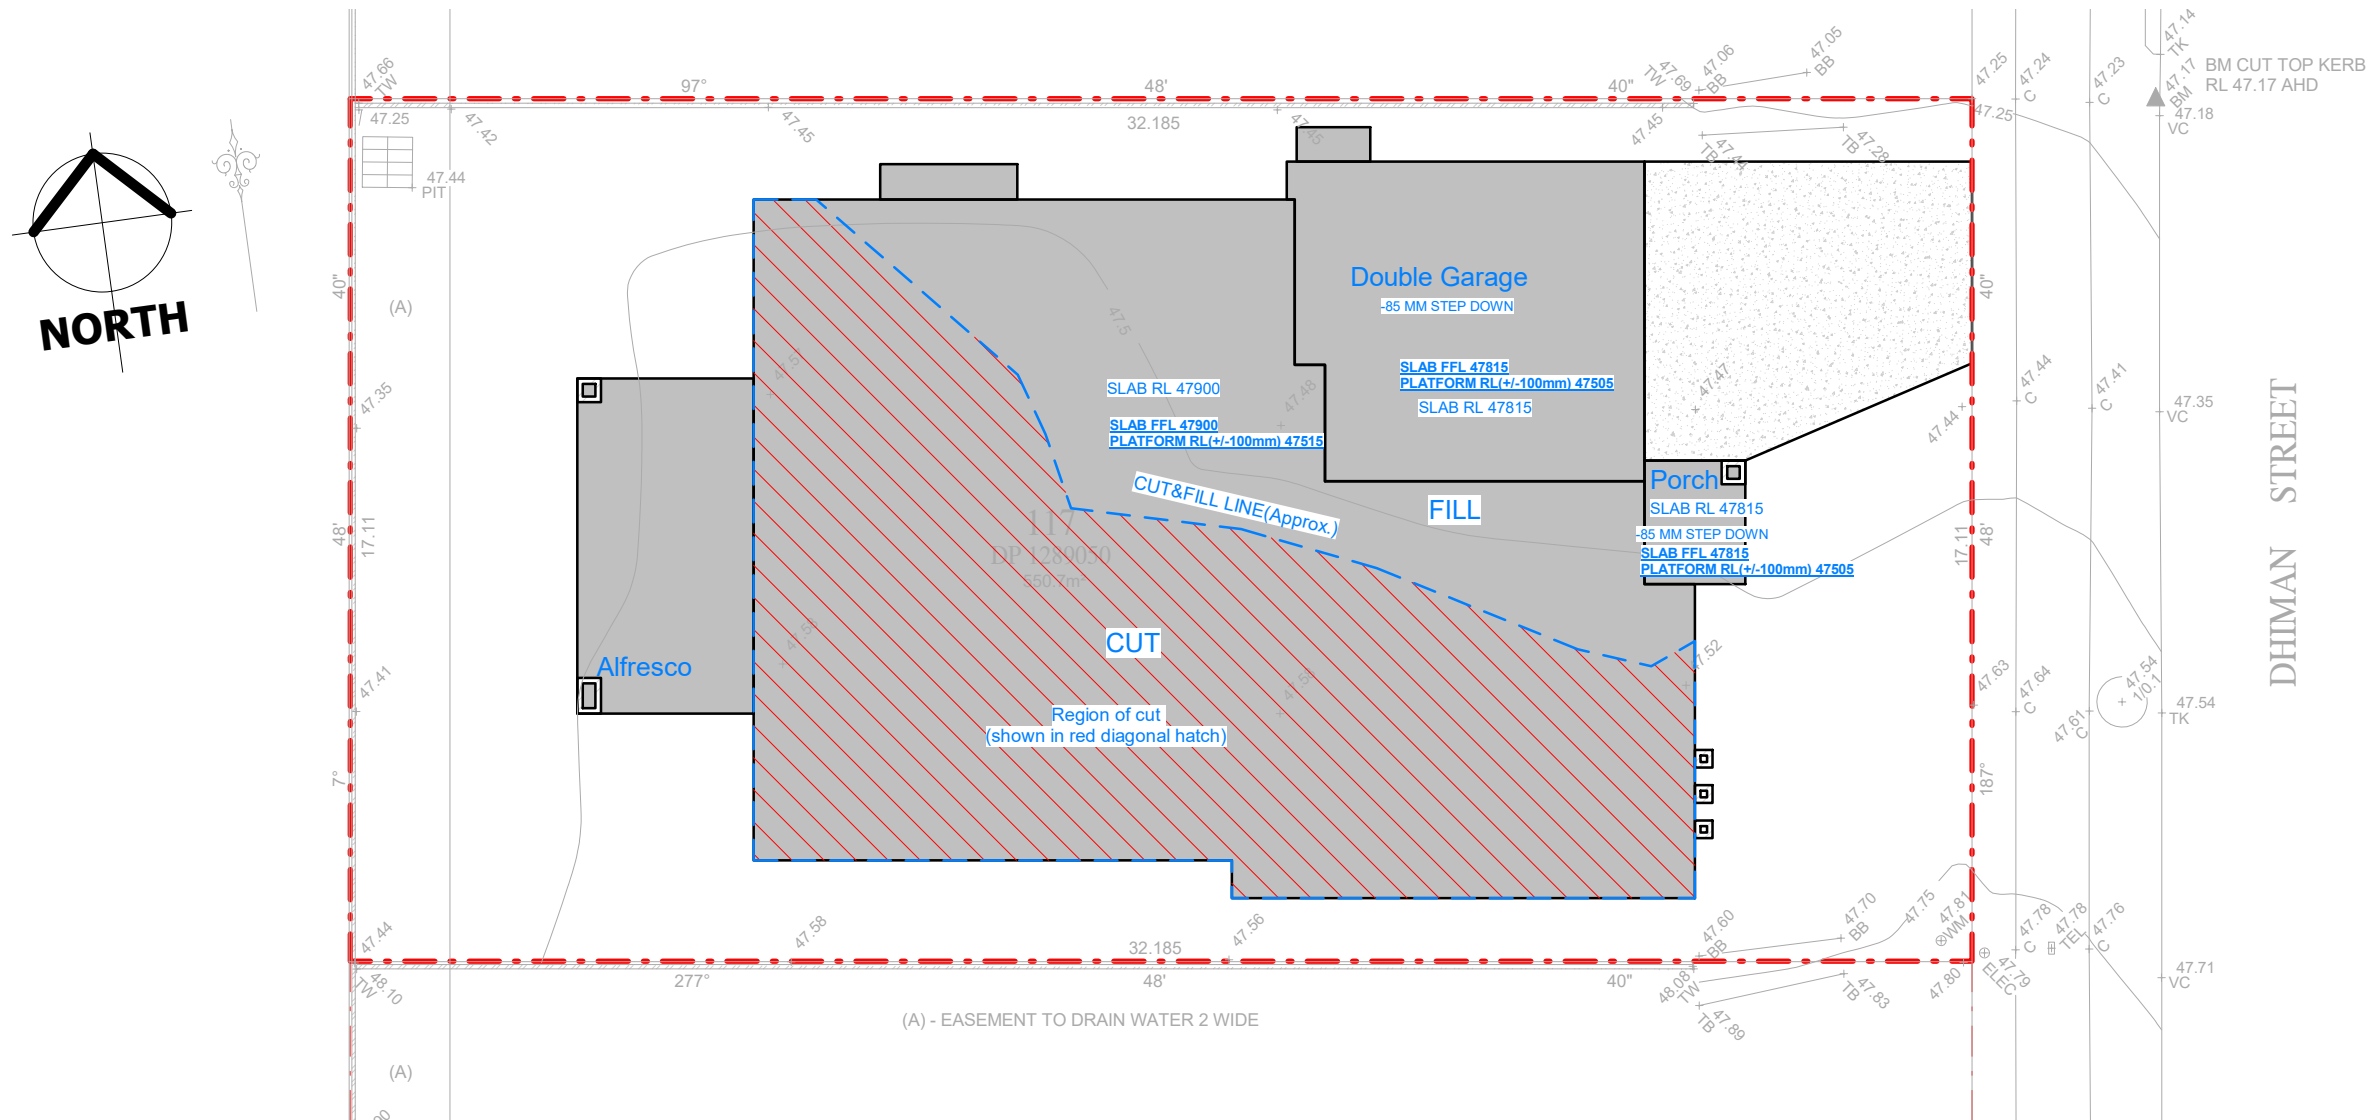

Cut & Fill Plan
1 : 150



MISTRY
DESIGNS

60 Weaver Street
Erskine Park, NSW 2759


m :0430657990
e :nish@nm3d.com.au



Disclaimer:

Do not scale drawings. Work off figured dimensions. Verify all dimensions on site. Report any discrepancy to the designer.

Design and documentation there of are copyright and remain the property of Mistry Designs and must not be used in anyway, wholly or in part without the written consent of the designer

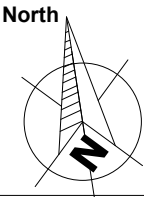

Drawing Title:
Cut & Fill Plan


Sheet No:
DA.101

Lodged at:	Penrith Council	Scale	1 : 150
Drawn by	VT	Date	26JULY2025

PROJECT :
Proposed Dwelling House


Address:
DHIMAN STREET, CLAREMONT MEADOWS
LOT 117

Job #MD1540 DA91			
C	Updated as per Council Requirements	NM	08.04.26
B	Updated as per Council Requirements	NM	22.03.26
A	Issue for DA	NM	25.11.25
Issue	Description	By	DATE

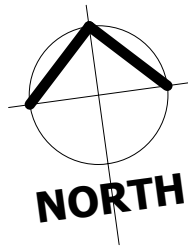

Ground Floor

1 : 100

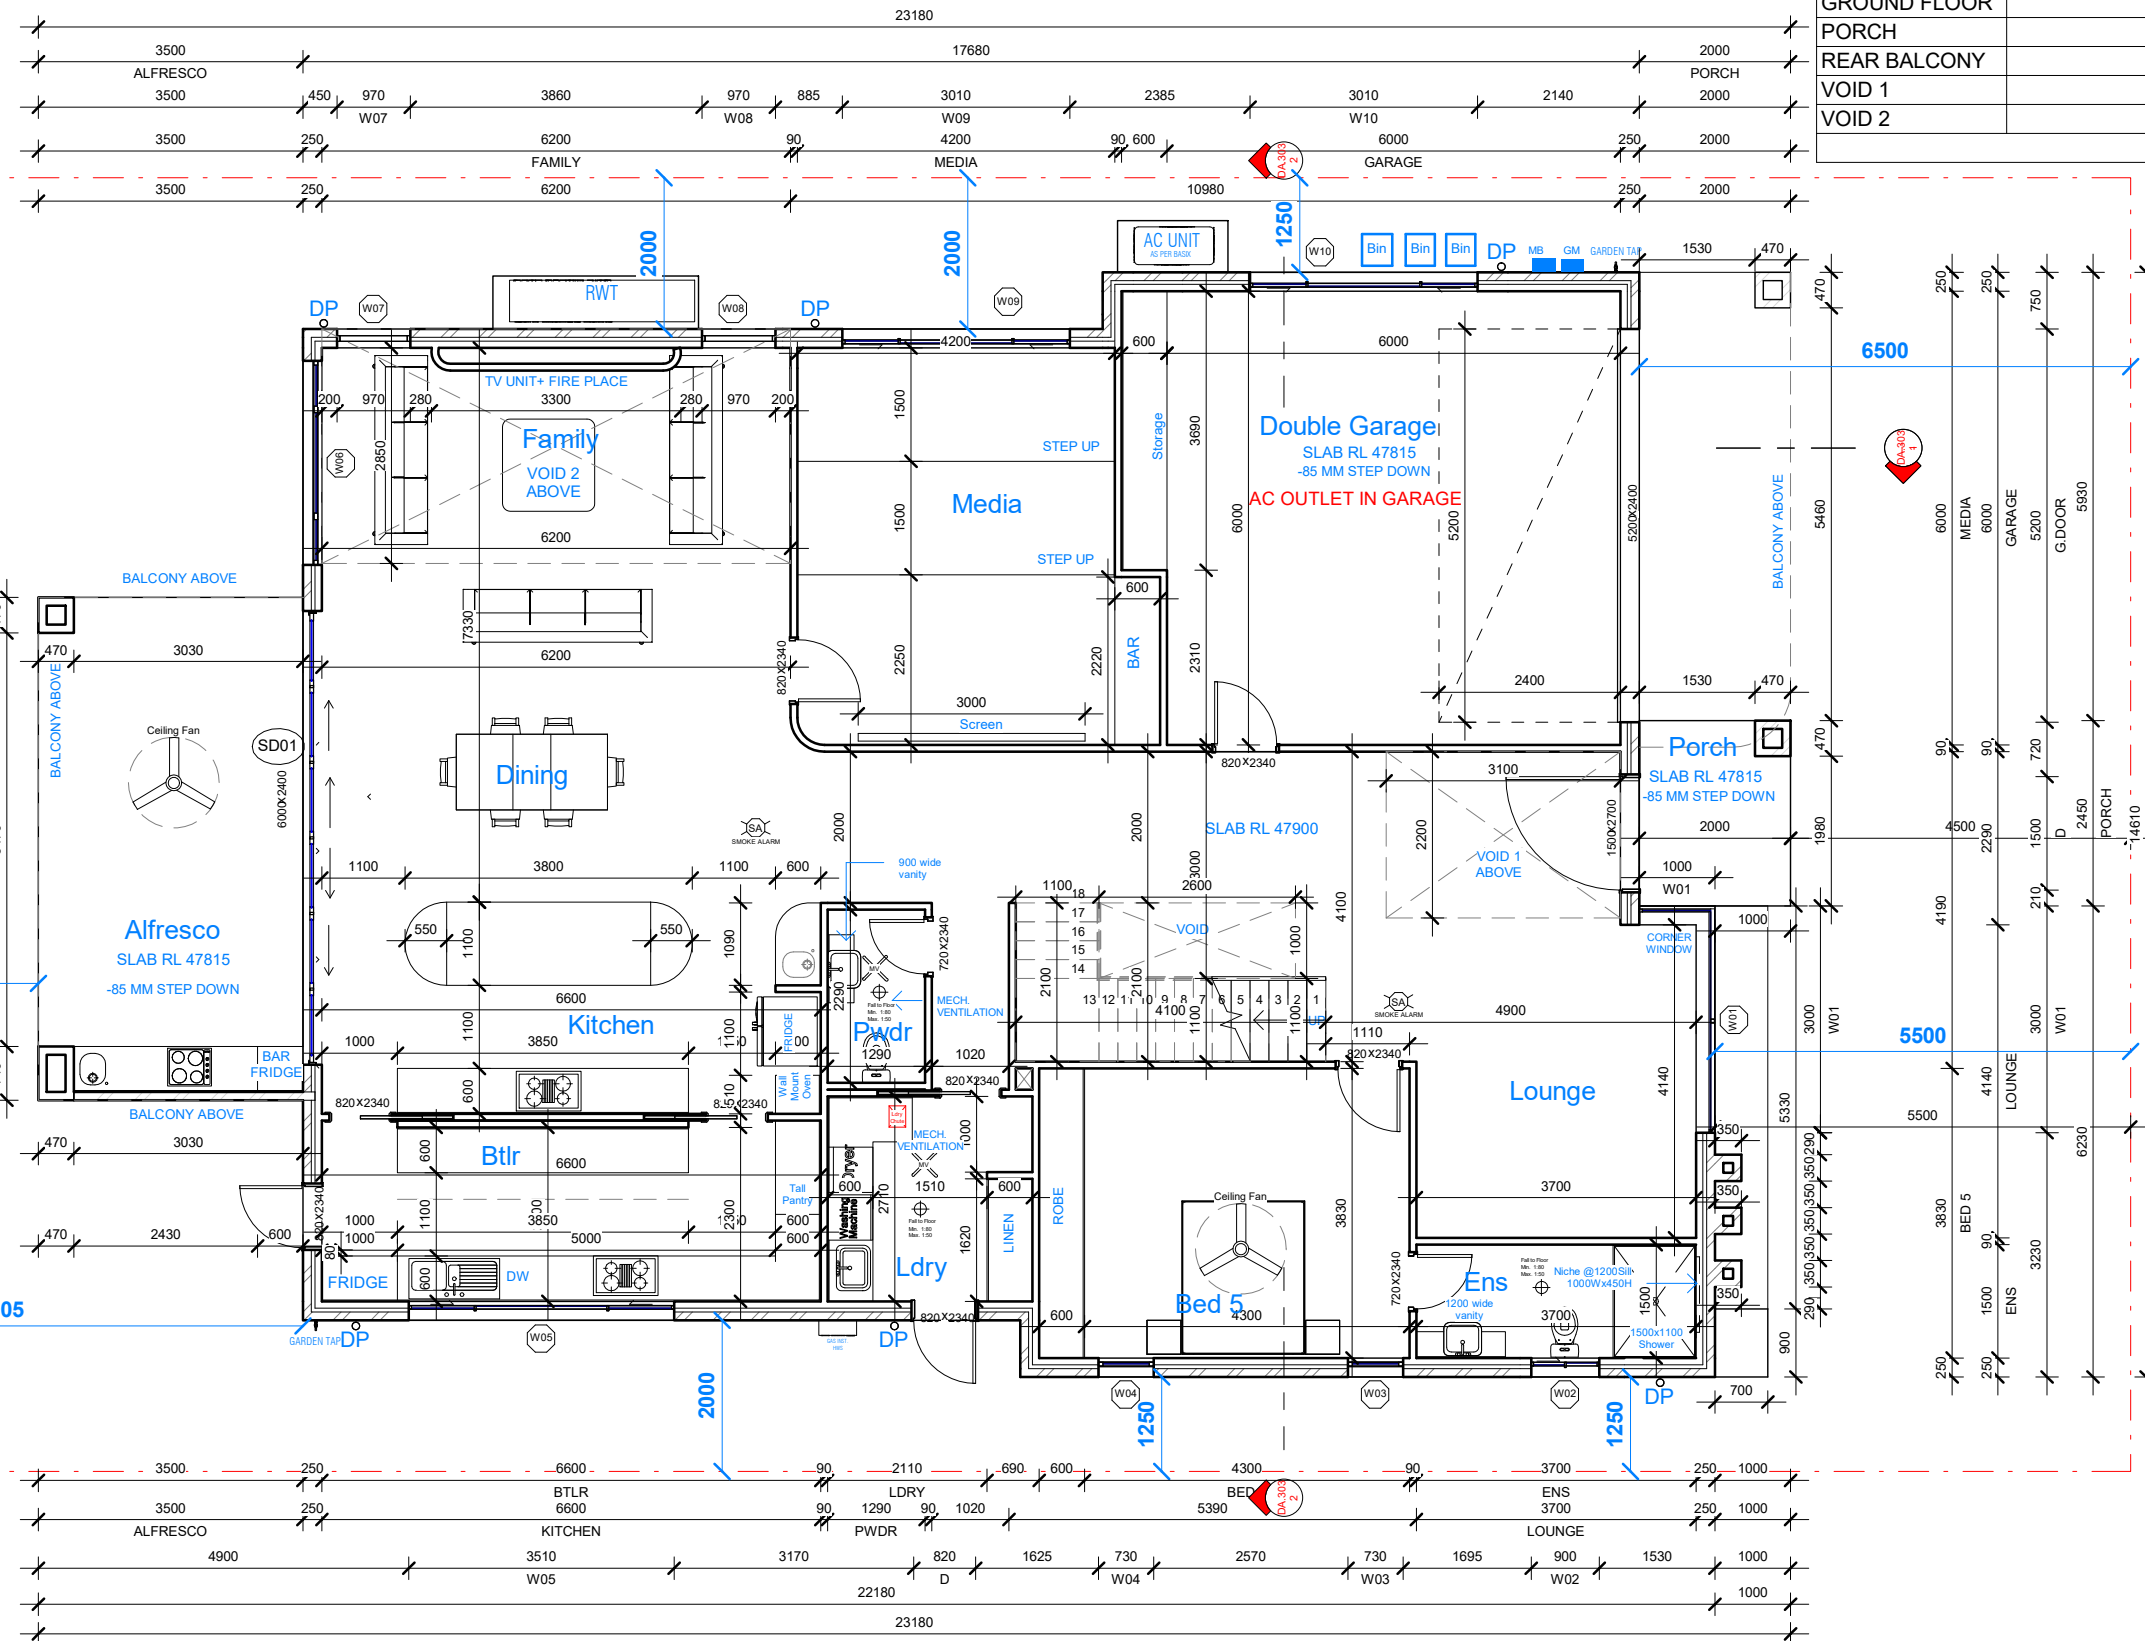

	S.q.m	Square
ALFRESCO	23.3 m ²	2.5
BALCONY	13.0 m ²	1.4
FIRST FLOOR	220.0 m ²	23.7
GARAGE	42.3 m ²	4.6
GROUND FLOOR	207.2 m ²	22.3
PORCH	4.9 m ²	0.5
REAR BALCONY	23.3 m ²	2.5
VOID 1	7.4 m ²	0.8
VOID 2	21.6 m ²	2.3
	563.0 m ²	60.6

LEGEND	
	FLOOR WASTE
	DOWN PIPE
	RAIN WATER TANK
	AIR-CONDITIONING OUTDOOR UNIT
	HOT WATER SYSTEM
	STORAGE BIN
	INTERCONNECTED SMOKE ALARM
	MECHANICAL EXHAUST

Job #MD1540 DA91



MISTRY
DESIGNS

60 Weaver Street
Erskine Park, NSW 2759

m :0430657990
e :nish@nm3d.com.au



Disclaimer:

Do not scale drawings. Work off figured dimensions. Verify all dimensions on site. Report any discrepancy to the designer.

Design and documentation there of are copyright and remain the property of Mistry Designs and must not be used in anyway, wholly or in part without the written consent of the designer



Drawing Title:
Ground Floor Plan


Sheet No:
DA.201

Lodged at:	Penrith Council	Scale	1 : 100
Drawn by	VT	Date	26JULY2025

PROJECT :
Proposed Dwelling House


Address:
DHIMAN STREET, CLAREMONT MEADOWS
LOT 117

C	Updated as per Council Requirements	NM	08.04.26
B	Updated as per Council Requirements	NM	22.03.26
A	Issue for DA	NM	25.11.25
Issue	Description	By	DATE

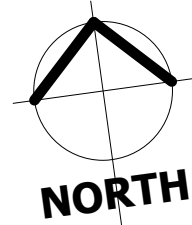

First Floor

1 : 100

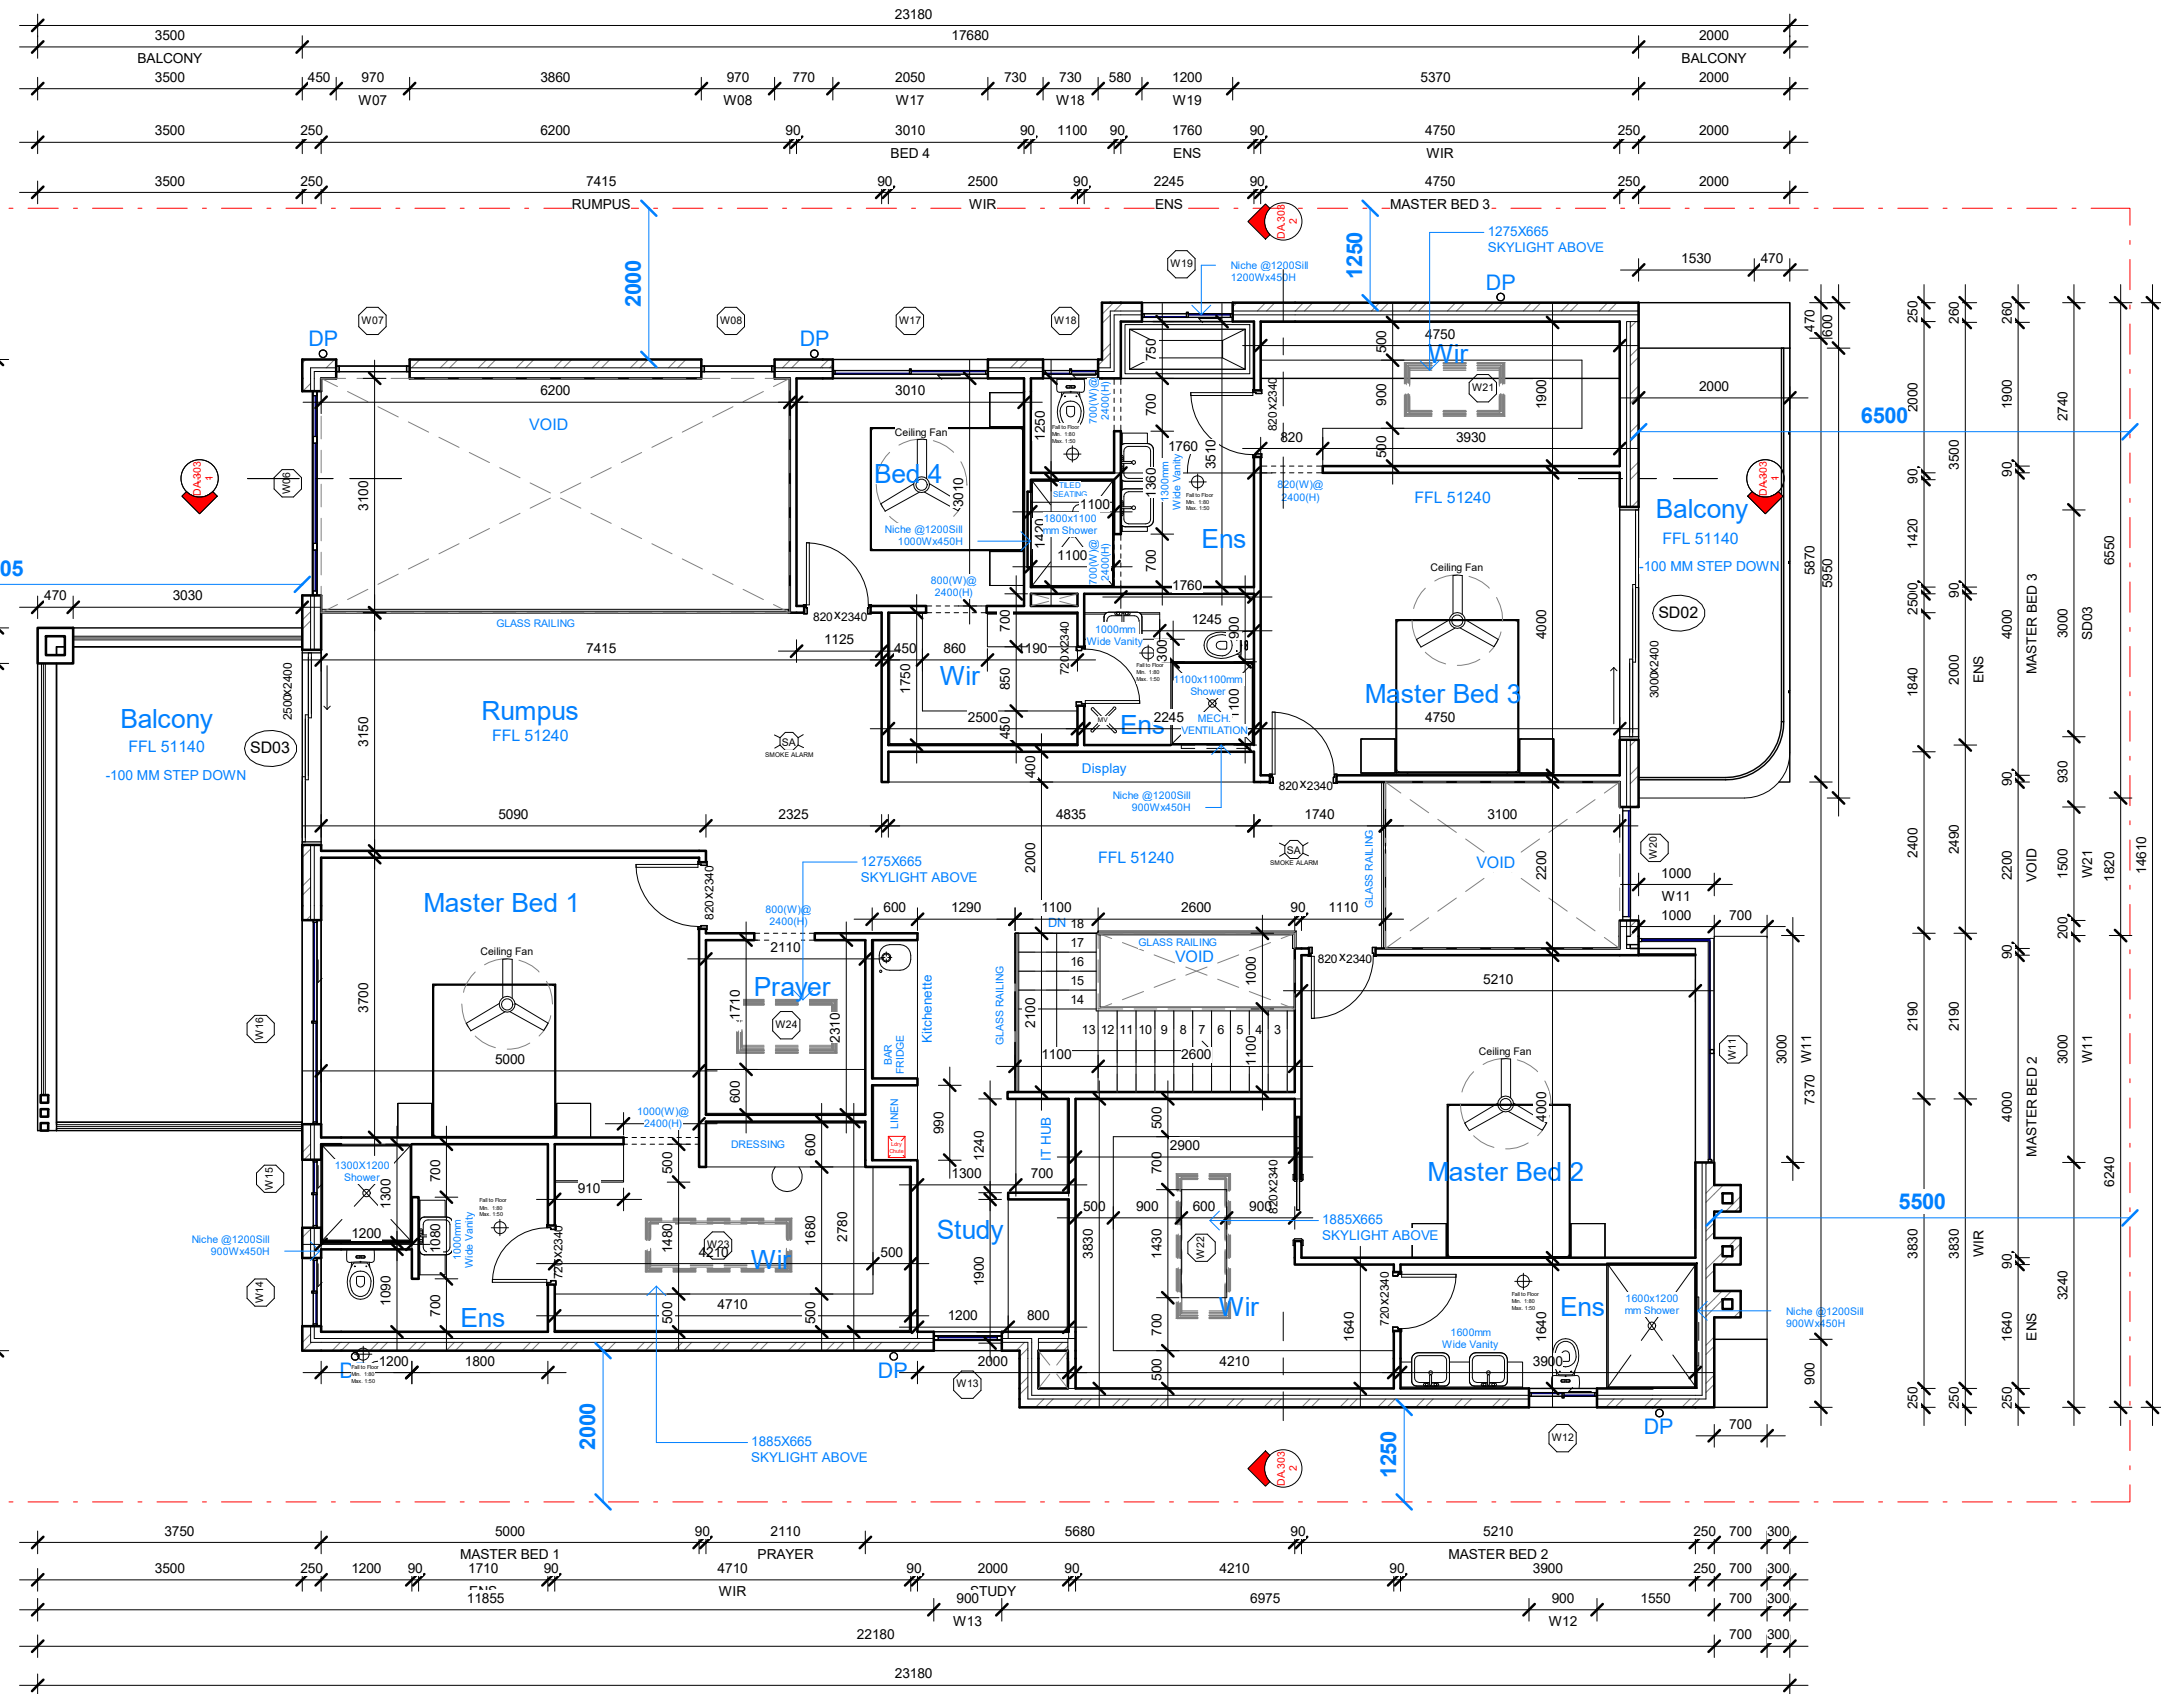

**MISTRY
DESIGNS**

60 Weaver Street
Erskine Park, NSW 2759
m :0430657990
e :nish@nm3d.com.au



Disclaimer:

Do not scale drawings. Work off figured dimensions. Verify all dimensions on site. Report any discrepancy to the designer.

Design and documentation there of are copyright and remain the property of Mistry Designs and must not be used in anyway, wholly or in part without the written consent of the designer



Drawing Title:
First Floor Plan

Sheet No:
DA.202


Lodged at:	Penrith Council	Scale	1 : 100
Drawn by	VT	Date	26JULY2025

PROJECT :
Proposed Dwelling House

Address:
DHIMAN STREET, CLAREMONT MEADOWS
LOT 117

Job #MD1540 DA91

C	Updated as per Council Requirements	NM	08.04.26
B	Updated as per Council Requirements	NM	22.03.26
A	Issue for DA	NM	25.11.25
Issue	Description	By	DATE

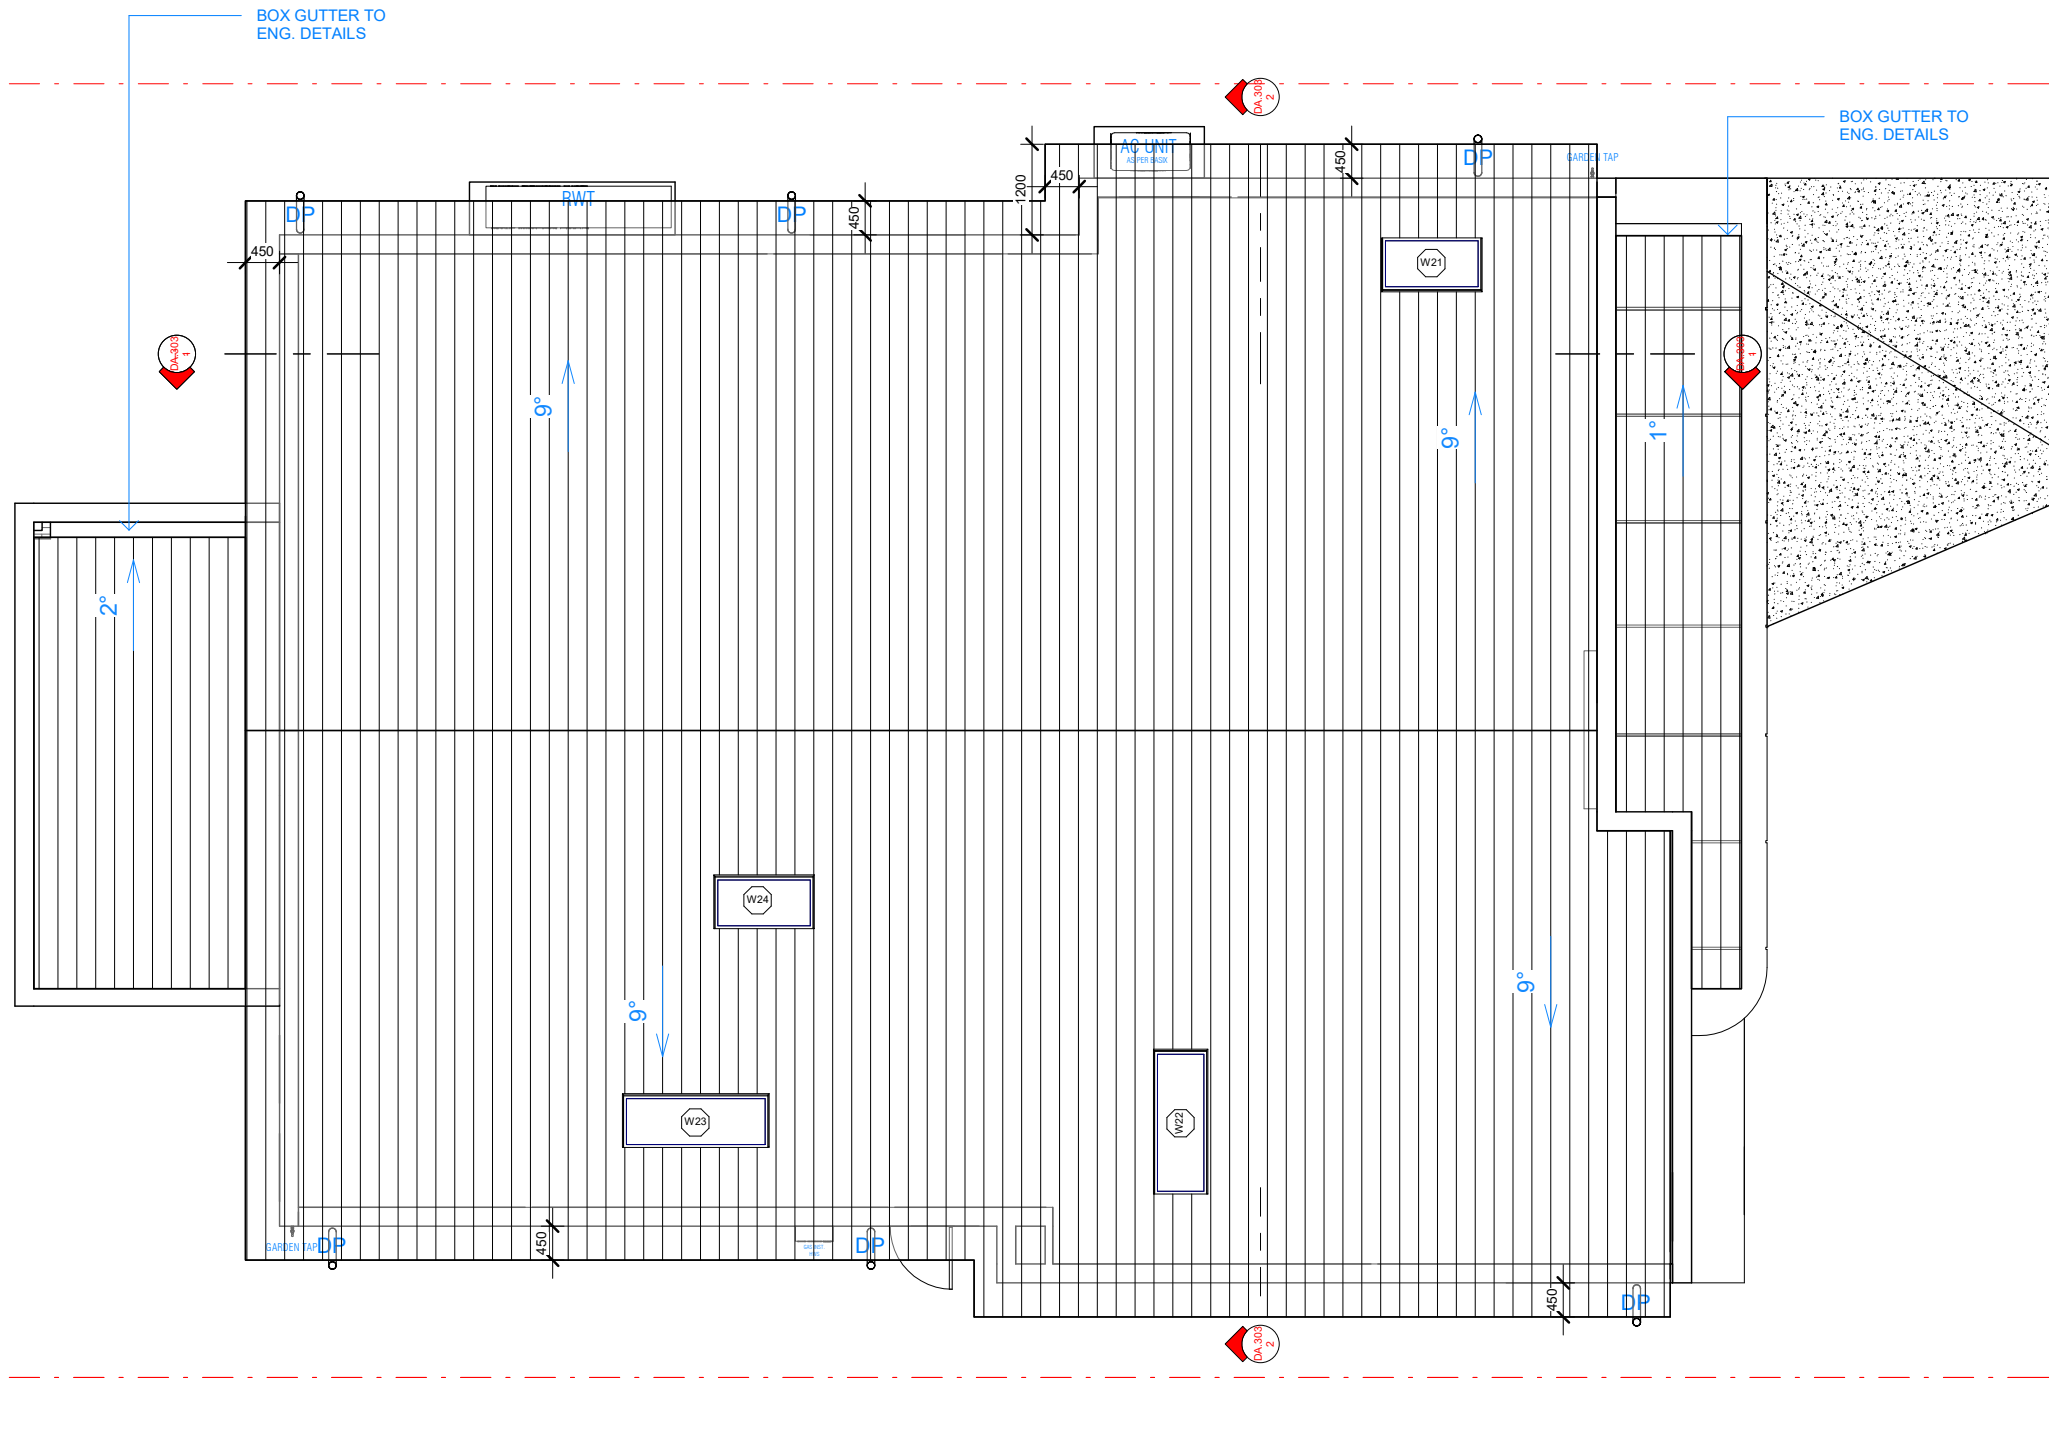

Roof Plan
1 : 100



**MISTRY
DESIGNS**

60 Weaver Street
Erskine Park, NSW 2759

m :0430657990
e :nish@nm3d.com.au



Disclaimer:

Do not scale drawings. Work off figured dimensions. Verify all dimensions on site. Report any discrepancy to the designer.

Design and documentation there of are copyright and remain the property of Mistry Designs and must not be used in anyway, wholly or in part without the written consent of the designer



Drawing Title:
Roof Plan

Sheet No:
DA.203

Lodged at:	Penrith Council	Scale	1 : 100
Drawn by	VT	Date	26JULY2025

PROJECT :


Proposed Dwelling House

Address:


DHIMAN STREET, CLAREMONT MEADOWS
LOT 117

Job #MD1540 DA91

C	Updated as per Council Requirements	NM	08.04.26
B	Updated as per Council Requirements	NM	22.03.26
A	Issue for DA	NM	25.11.25
Issue	Description	By	DATE

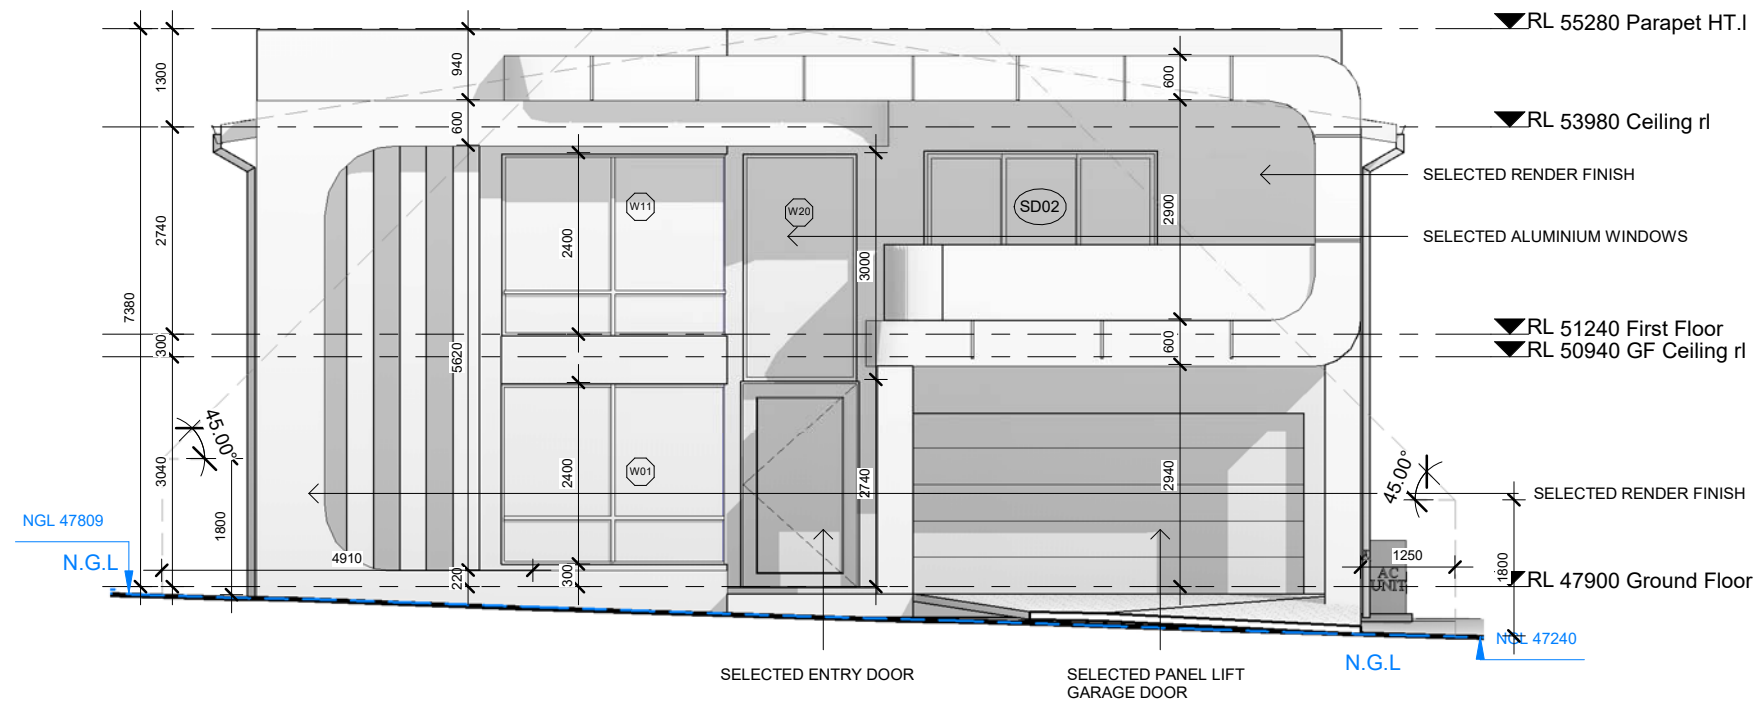

EAST ELEVATION
1 : 100

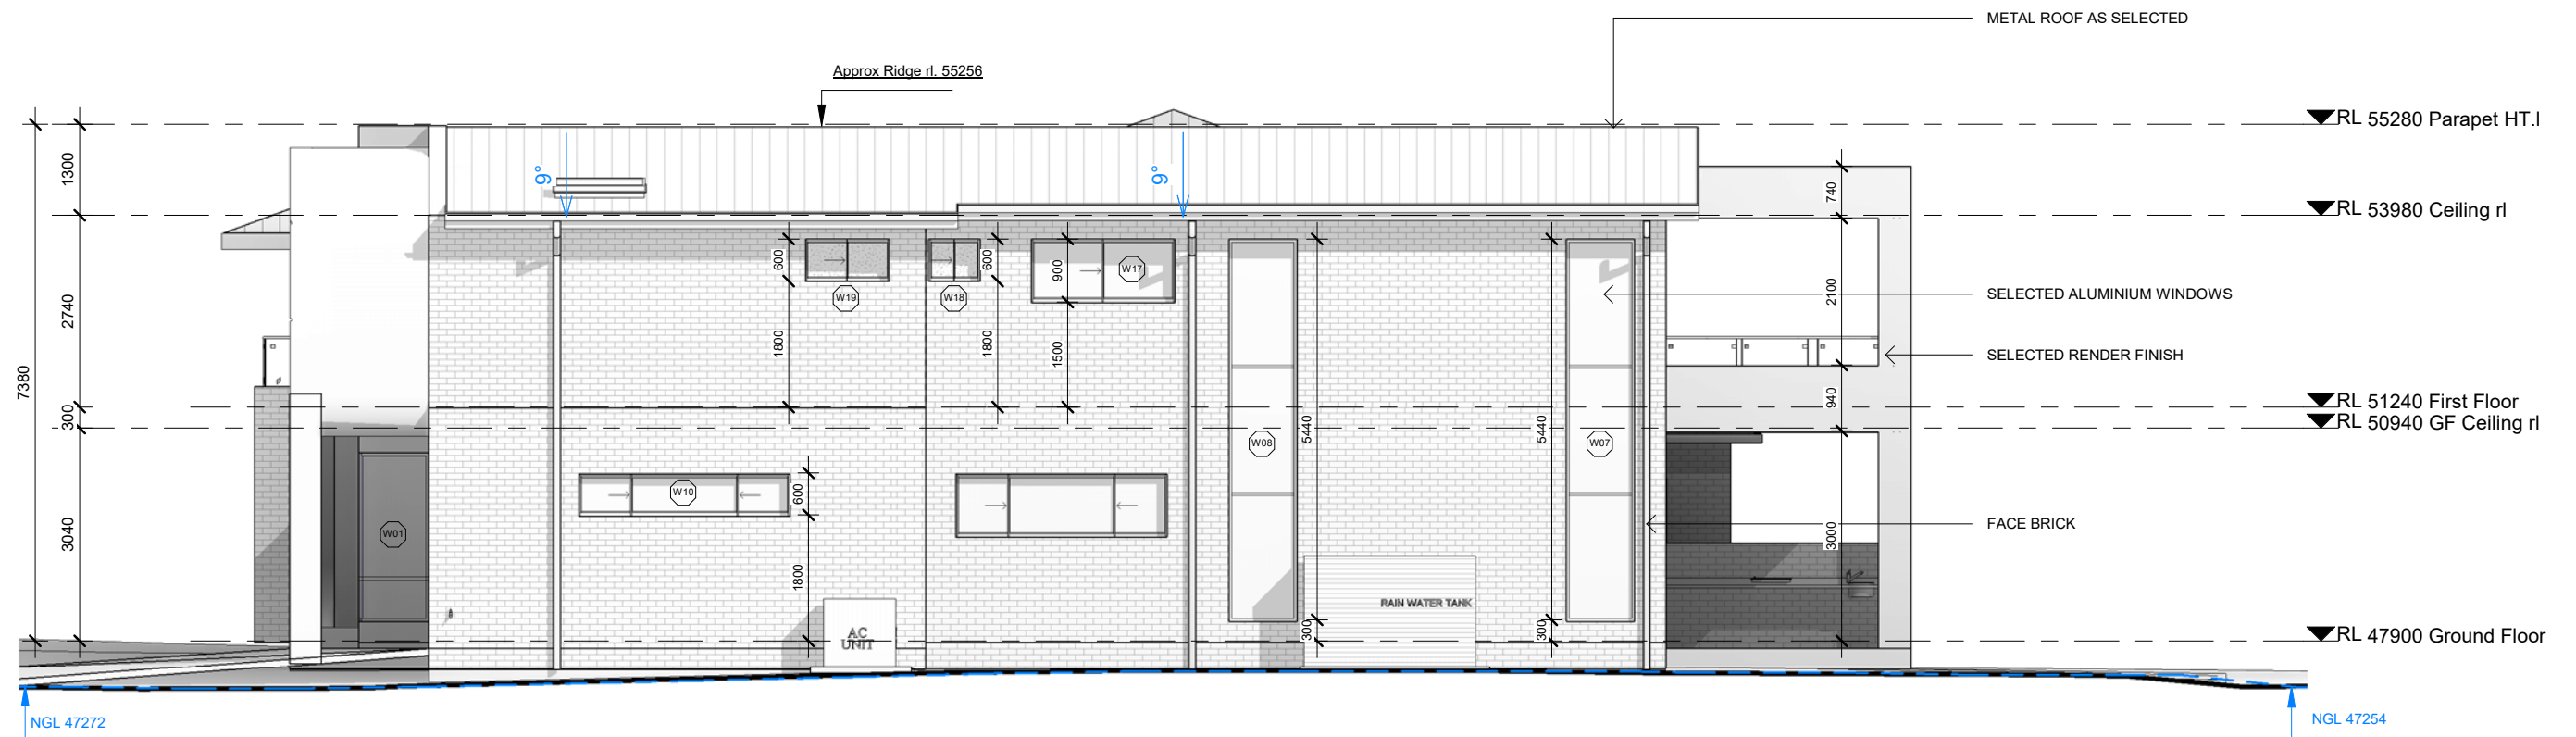

NORTH ELEVATION
1 : 100



**MISTRY
DESIGNS**

60 Weaver Street
Erskine Park, NSW 2759

m :0430657990
e :nish@nm3d.com.au



Disclaimer:

Do not scale drawings. Work off figured dimensions. Verify all dimensions on site. Report any discrepancy to the designer.

Design and documentation there of are copyright and remain the property of Mistry Designs and must not be used in anyway, wholly or in part without the written consent of the designer



Drawing Title:
Elevations

Sheet No:
DA.300

Lodged at:	Penrith Council	Scale	1 : 100
Drawn by	VT	Date	26JULY2025

PROJECT :


Proposed Dwelling House

Address:


DHIMAN STREET, CLAREMONT MEADOWS
LOT 117

Job #MD1540 DA91


C	Updated as per Council Requirements	NM	08.04.26
B	Updated as per Council Requirements	NM	22.03.26
A	Issue for DA	NM	25.11.25
Issue	Description	By	DATE

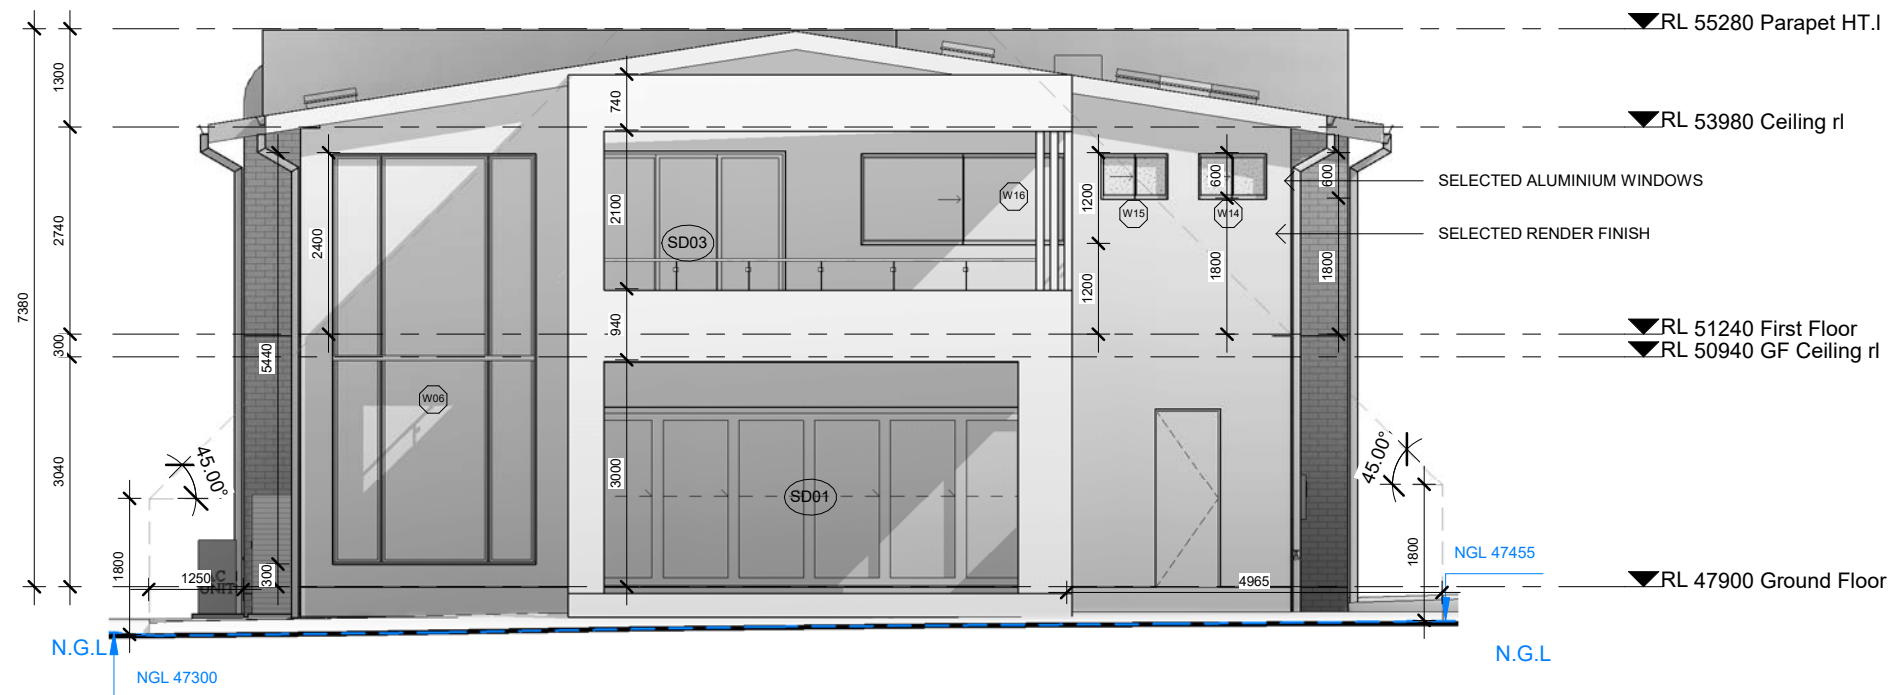


WEST ELEVATION
1 : 100

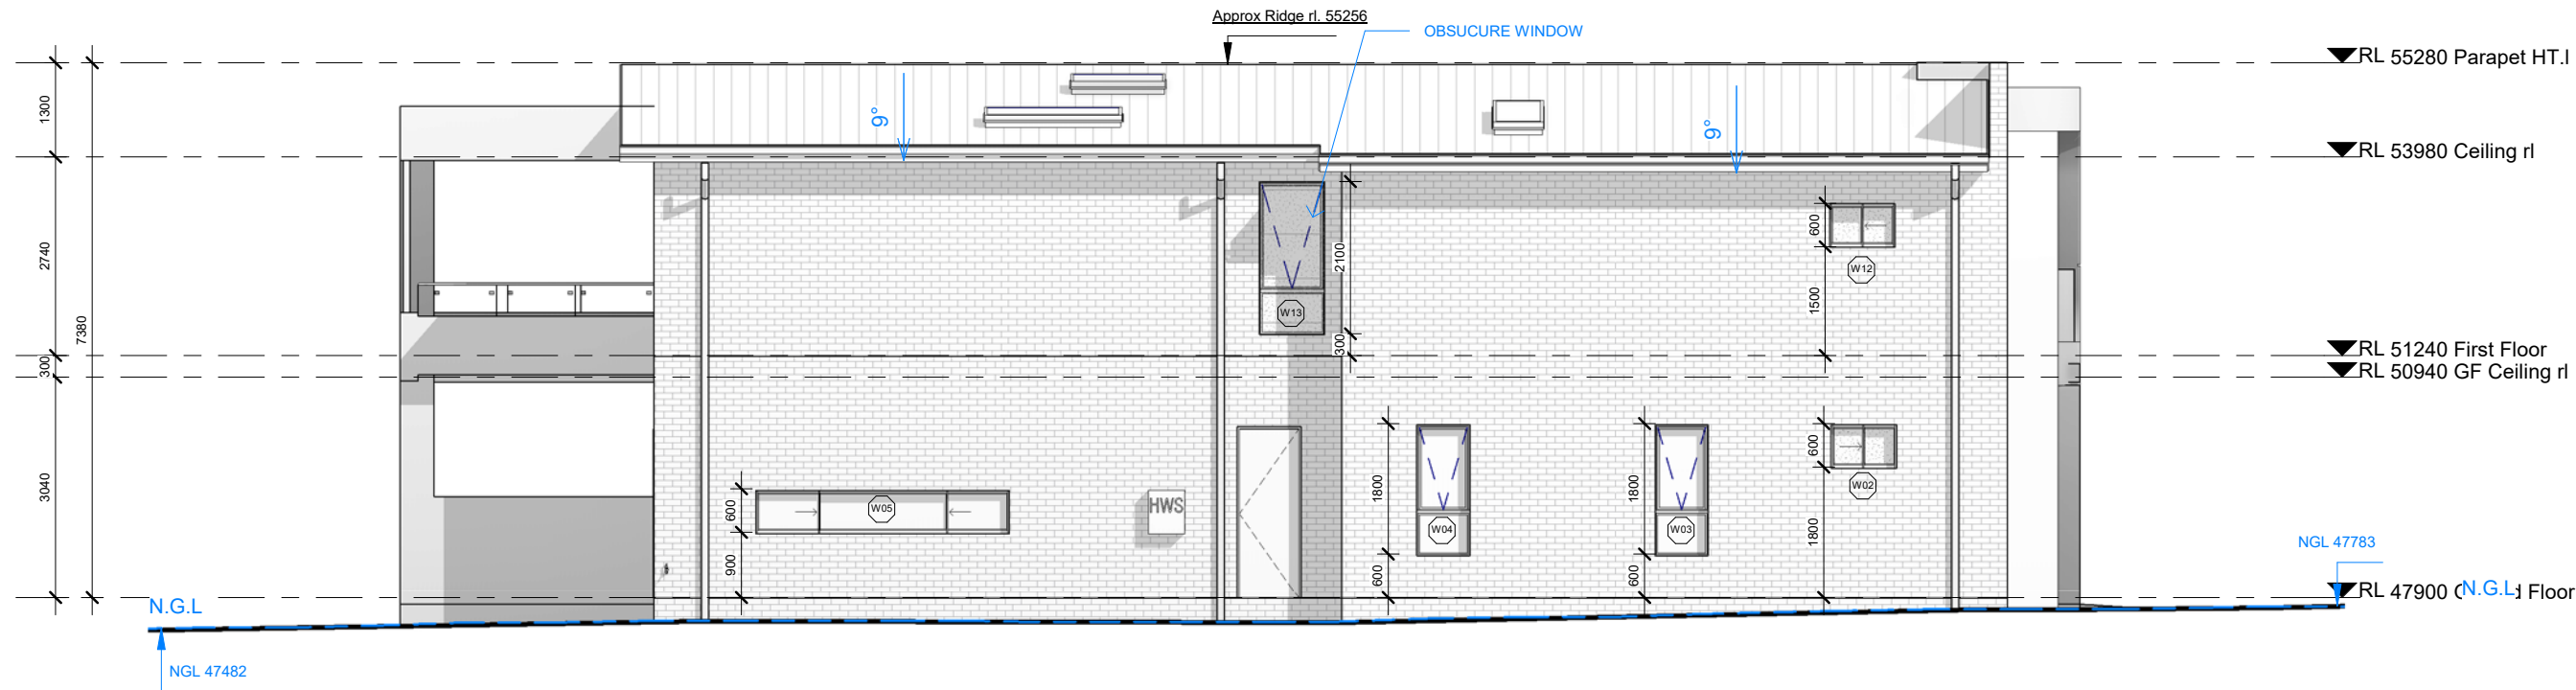

SOUTH ELEVATION
1 : 100

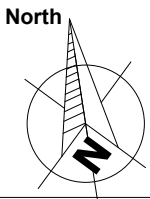


C	Updated as per Council Requirements	NM	08.04.26
B	Updated as per Council Requirements	NM	22.03.26
A	Issue for DA	NM	25.11.25
Issue	Description	By	DATE

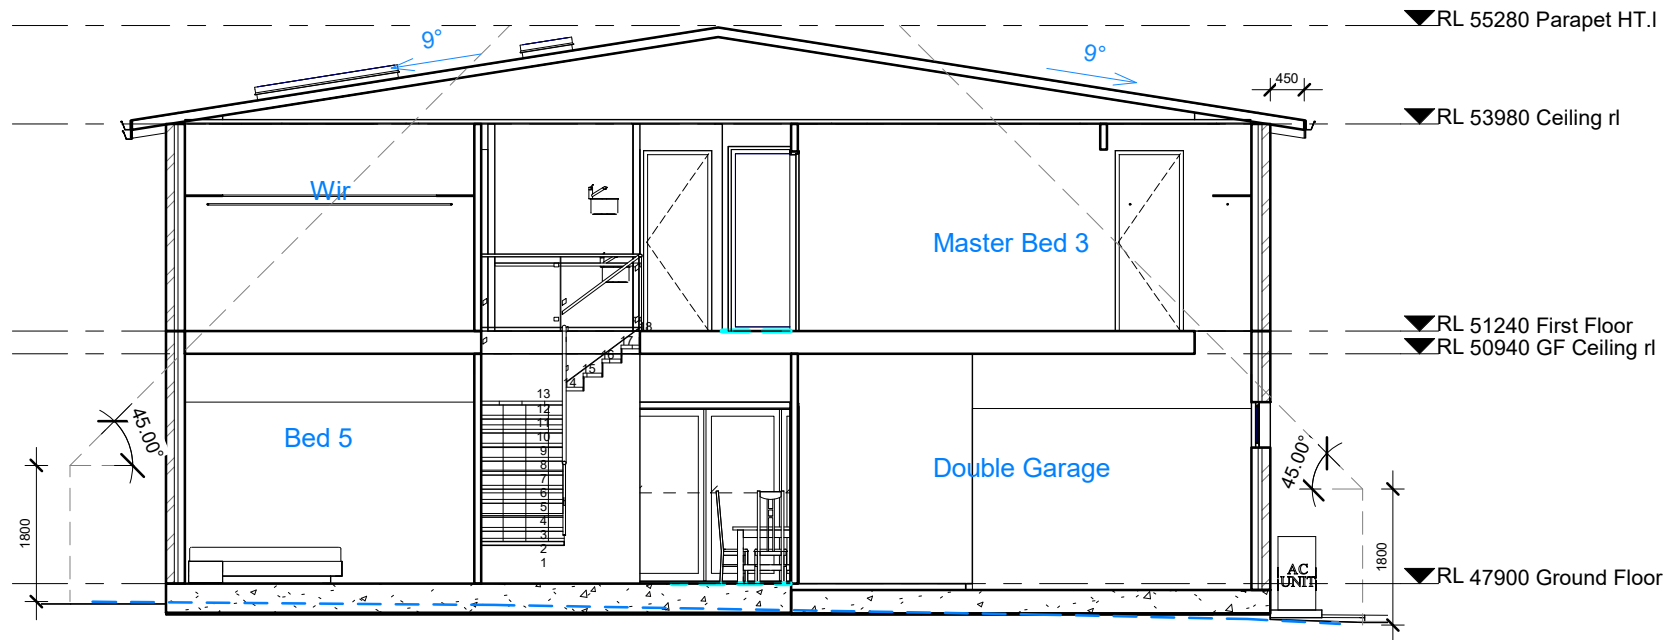

Section 1
1 : 100

O- OBSECURE GLAZING		Window Schedule		W01 AND W11 ARE CORNER WINDOW		
Mark	Level	Type	Size		Sill Height	Head Height
			Height	Width		
W01	Ground Floor	F-CORNER	2400	3000 X1000	300	2700
W02	Ground Floor	O-S-F	600	900	1800	2400
W03	Ground Floor	A-F	1800	730	600	2400
W04	Ground Floor	A-F	1800	730	600	2400
W05	Ground Floor	S-F-S	600	3510	900	1500
W06	Ground Floor	F-F-F	5440	2700	300	5740
W07	Ground Floor	F-F-F	5440	970	300	5740
W08	Ground Floor	F-F-F	5440	970	300	5740
W09	Ground Floor	S-F-S	900	3010	1500	2400
W10	Ground Floor	S-F-S	600	3010	1800	2400
W11	First Floor	F-CORNER	2400	3000 X1000	0	2400
W12	First Floor	O-S-F	600	900	1500	2100
W13	First Floor	O-A-F	2100	900	300	2400
W14	First Floor	O-S-F	600	900	1800	2400
W15	First Floor	O-S-F	600	900	1800	2400
W16	First Floor	S-F	1200	2700	1200	2400
W17	First Floor	S-F	900	2050	1500	2400
W18	First Floor	O-S-F	600	730	1800	2400
W19	First Floor	O-S-F	600	1200	1800	2400
W20	Ground Floor	F	3000	1500	2740	5740
W21	First Floor	SKYLIGHT	665	1275		
W22	First Floor	SKYLIGHT	665	1885		
W23	First Floor	SKYLIGHT	665	1885		
W24	First Floor	SKYLIGHT	665	1275		

Door Schedule			
Mark	Level	Size	
		Height	Width
SD01	Ground Floor	2400	6000
SD02	First Floor	2400	3000
SD03	First Floor	2400	2500
Grand total: 3			

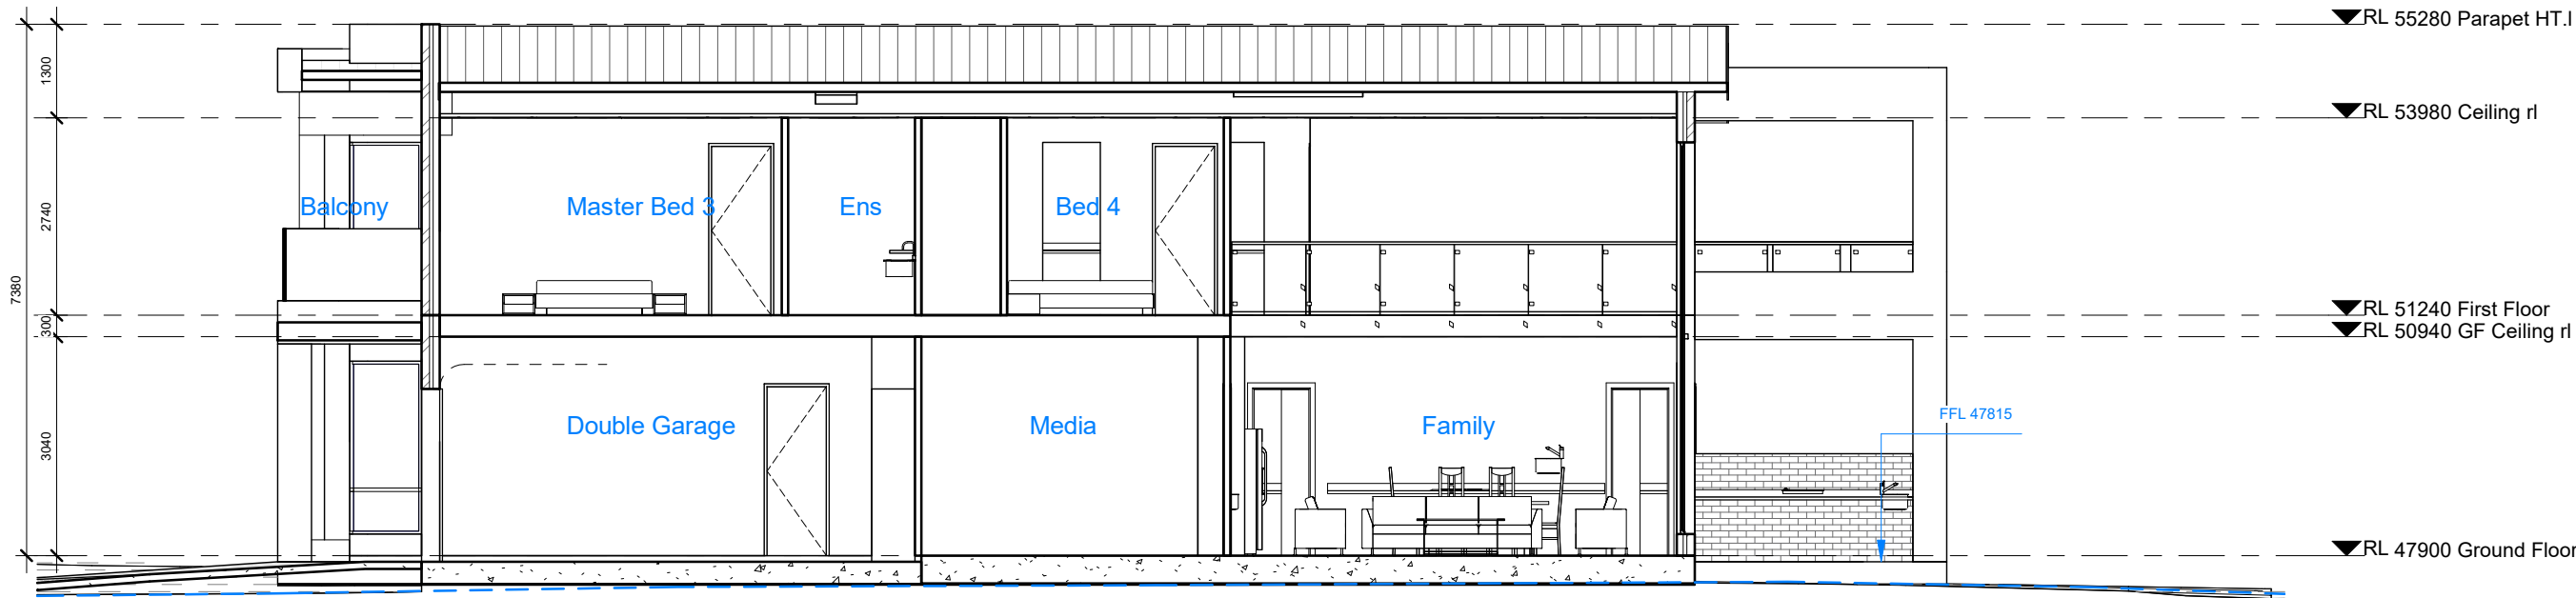

Section 2
1 : 100




MISTRY
DESIGNS

60 Weaver Street
Erskine Park, NSW 2759
m :0430657990
e :nish@nm3d.com.au



Disclaimer:
Do not sclae drawings. Work off figured dimensions.Verify all dimensions on site. Report any discrepancy to the designer.
Design and documentation there of are copyright and remain the property of Mistry Designs and must not be used in anyway, wholly or in part without the written consent of the designer

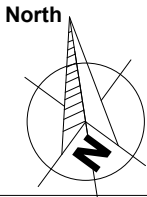

Drawing Title:
Sections/Window Schedule

Sheet No:
DA.303




Lodged at:	Penrith Council	Scale	1 : 100
Drawn by	VT	Date	26JULY2025

PROJECT :
Proposed Dwelling House

Address:
DHIMAN STREET, CLAREMONT MEADOWS
LOT 117

Job #MD1540 DA91

C	Updated as per Council Requirements	NM	08.04.26
B	Updated as per Council Requirements	NM	22.03.26
A	Issue for DA	NM	25.11.25
Issue	Description	By	DATE

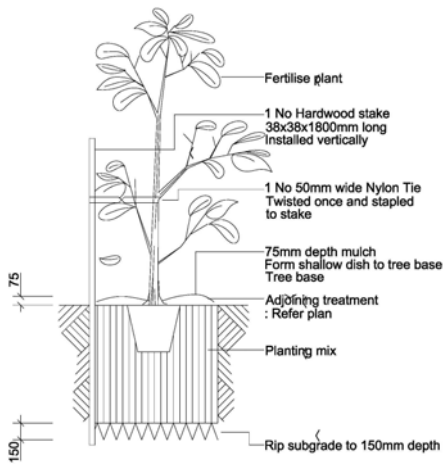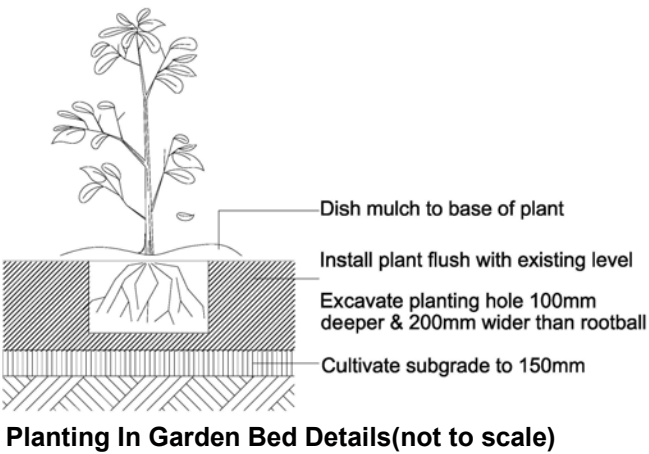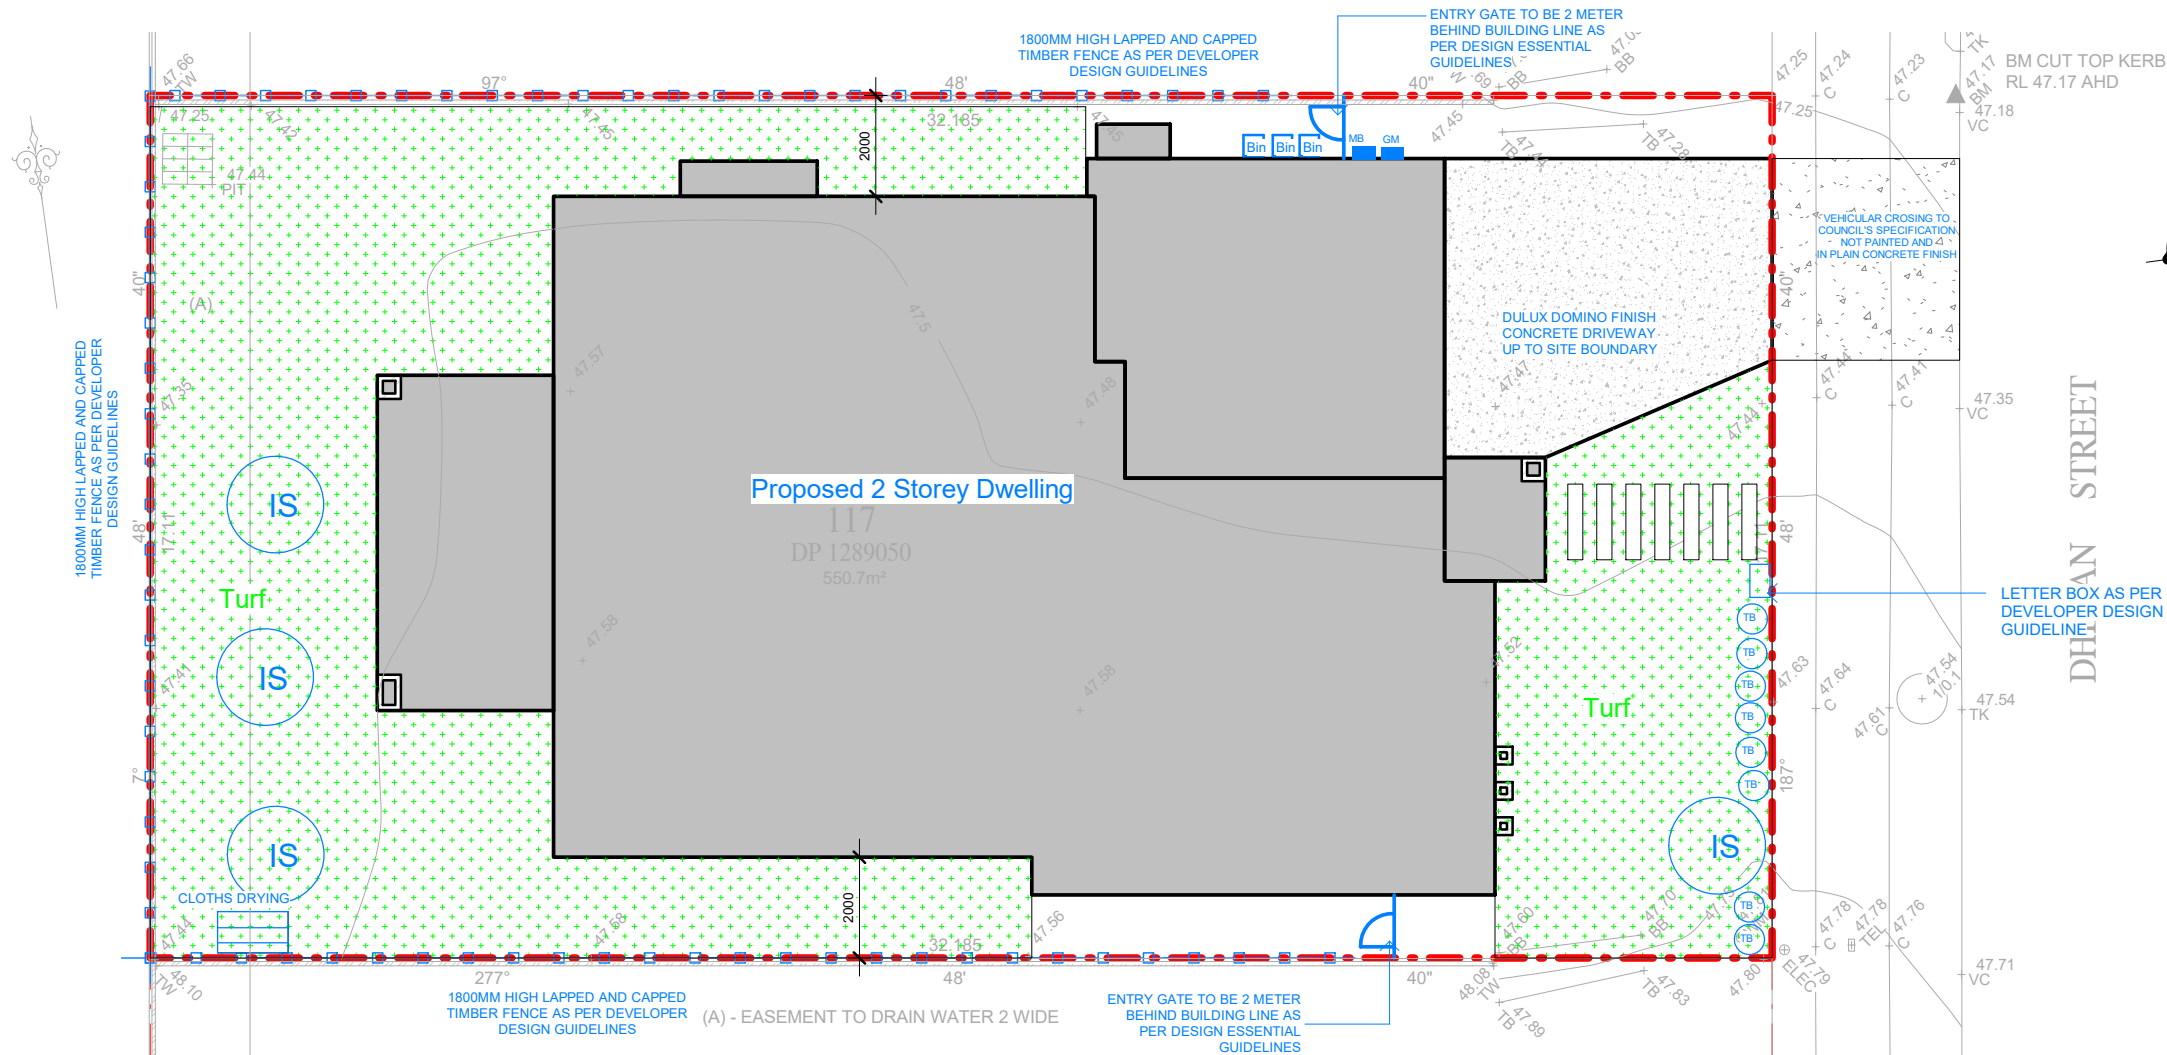

Landscape Plan

1 : 150



Turf



Selected Pebbles

TB

Tristaniopsis Burgundy blush PBR

IS

Indian Sumer White Weeping Crepe Myrtle(45L Pot Size)



Selected Brick Garden Edging

PLANTING SCHDULE

Description	Plant Names	Botanical Names	Image	Height	Pot Size	Quantity
TB	Tristaniopsis Burgundy blush PBR	Myrtaceae Tristaniopsis		1.5 -2m		8
IS	Indian Sumer White Weeping Crepe Myrtle(45L Pot Size)	Crepe Myrtle Lagerstroemia		4m	45L	4



MISTRY
DESIGNS


60 Weaver Street
Erskine Park, NSW 2759
m :0430657990
e :nish@nm3d.com.au



Disclaimer:

Do not sclae drawings. Work off figured dimensions. Verify all dimensions on site. Report any discrepancy to the designer.

Design and documentation there of are copyright and remain the property of Mistry Designs and must not be used in anyway, wholly or in part without the written consent of the designer

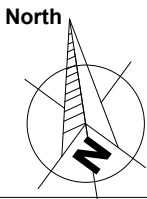

Drawing Title:
Concept Landscape Plan

Sheet No:
DA.400


Lodged at:	Penrith Council	Scale	As indicated
Drawn by	VT	Date	26JULY2025

PROJECT :
Proposed Dwelling House

Address:
DHIMAN STREET, CLAREMONT MEADOWS
LOT 117

Job #MD1540 DA91

C	Updated as per Council Requirements	NM	08.04.26
B	Updated as per Council Requirements	NM	22.03.26
A	Issue for DA	NM	25.11.25
Issue	Description	By	DATE

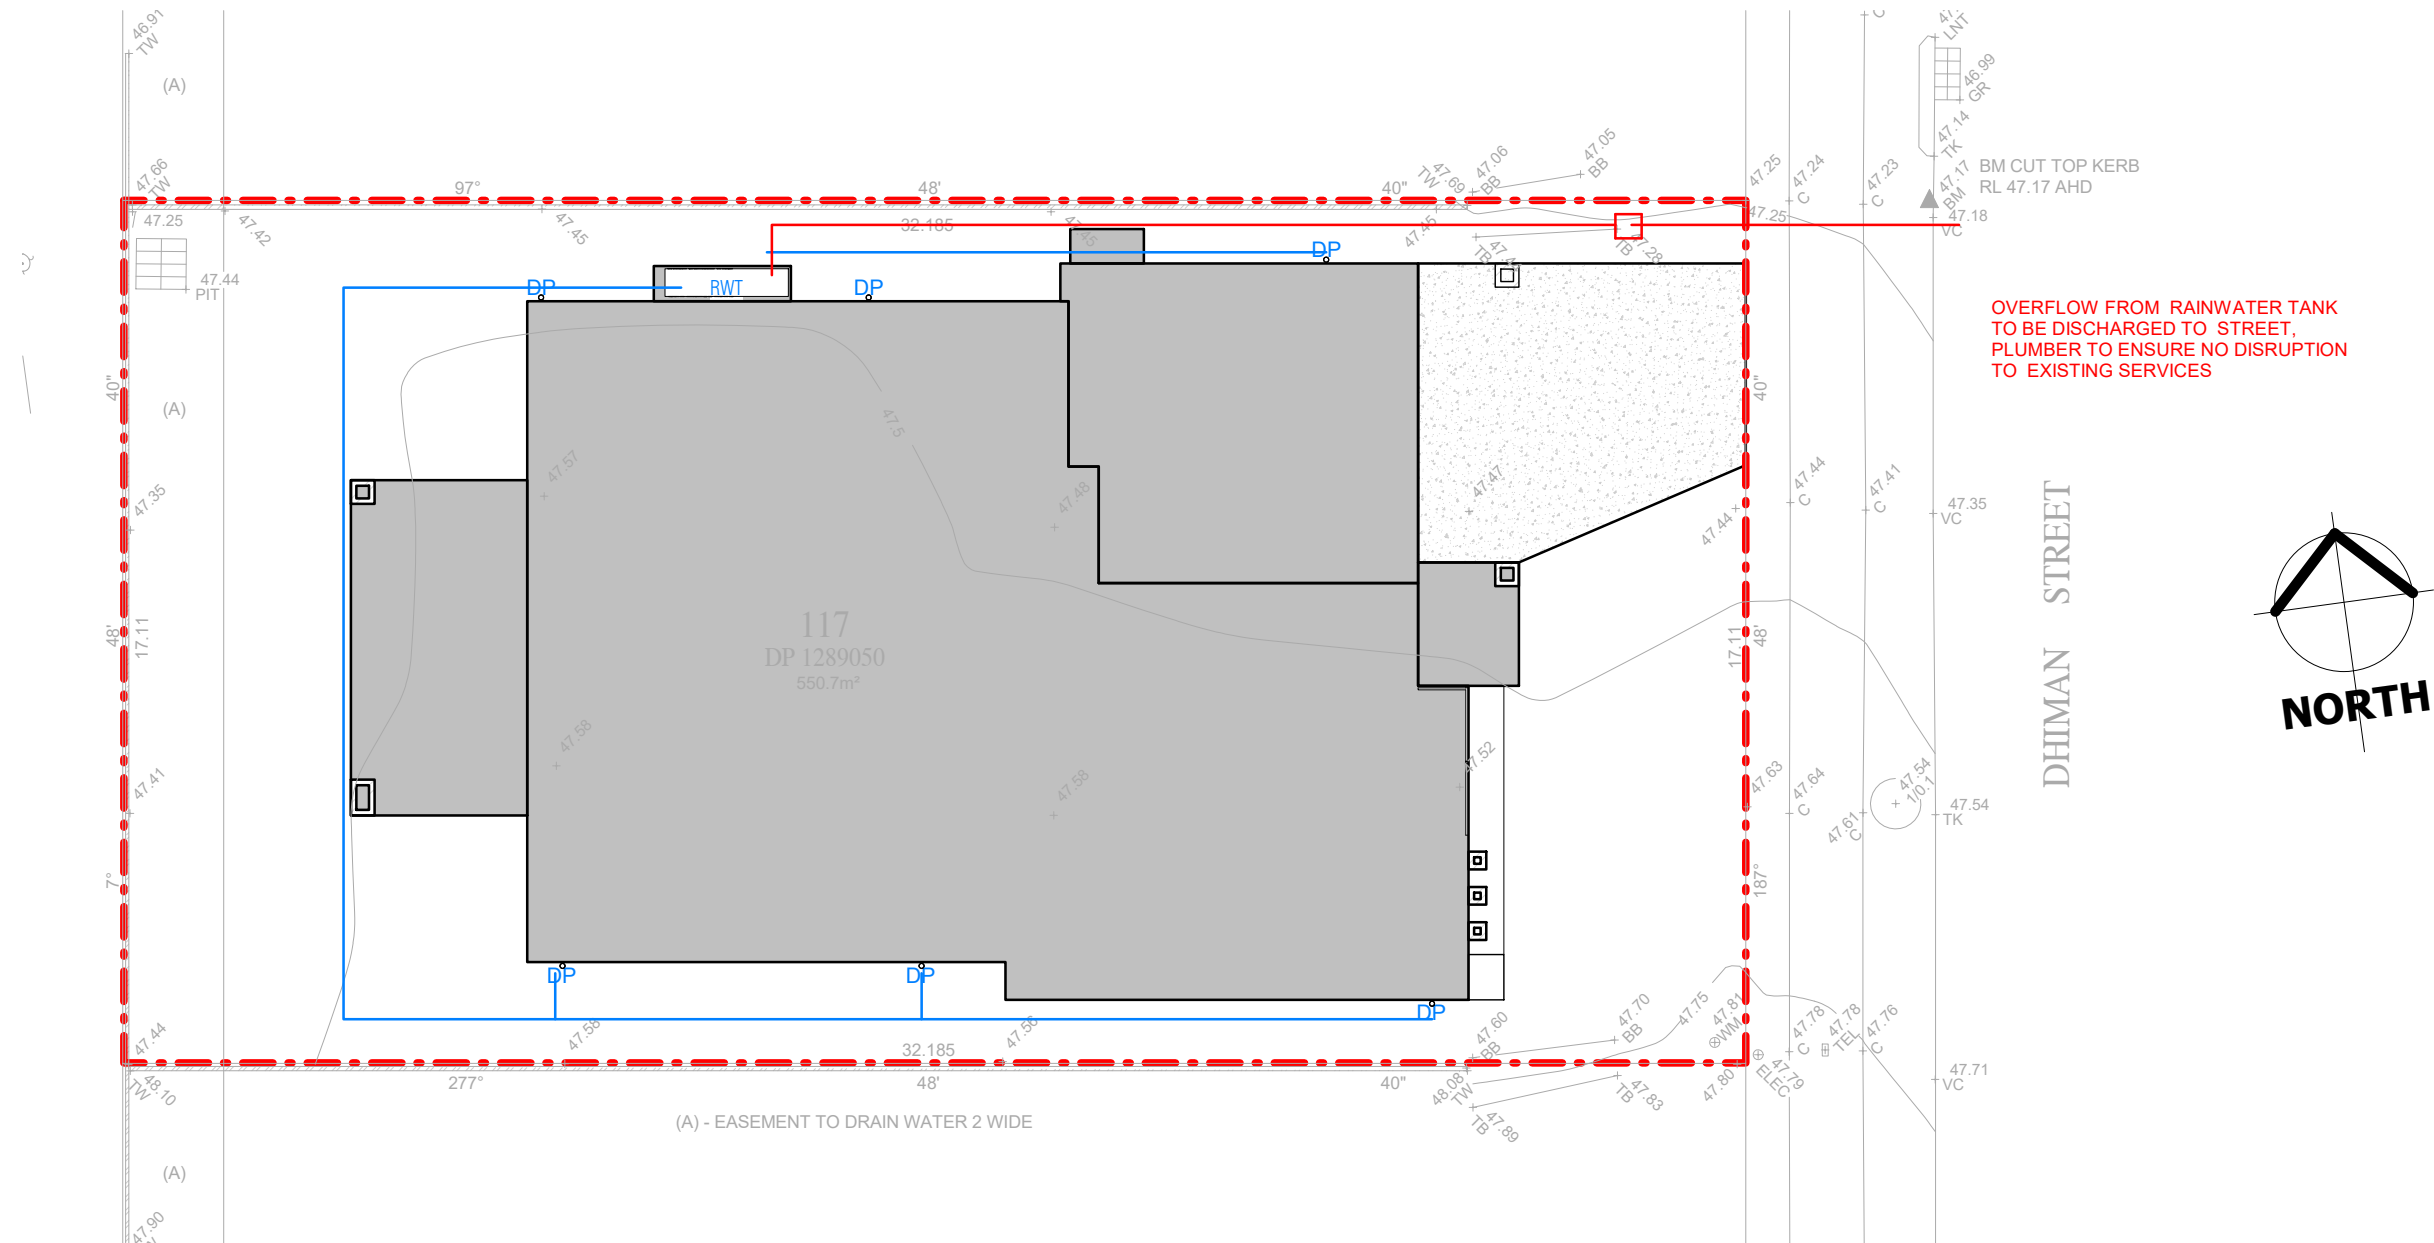

Concept Stormwater Plan

1 : 150

LEGEND:	
	OVERFLOW FROM RWT & STORMWATER LINES
	DOWN PIPE
	RAIN WATER TANK AS PER BASIX
	SURFACE DRAIN
	FLOW WATER DIRECTION IN PIPES Ø100 PVC



**MISTRY
DESIGNS**

60 Weaver Street
Erskine Park, NSW 2759

m :0430657990
e :nish@nm3d.com.au



Disclaimer:

Do not scale drawings. Work off figured dimensions. Verify all dimensions on site. Report any discrepancy to the designer.

Design and documentation there of are copyright and remain the property of Mistry Designs and must not be used in anyway, wholly or in part without the written consent of the designer



Drawing Title:
Concept Stormwater Plan

Sheet No:
DA.500



Lodged at:	Penrith Council	Scale	As indicated
Drawn by	VT	Date	26JULY2025

PROJECT :
Proposed Dwelling House


Address:
DHIMAN STREET, CLAREMONT MEADOWS
LOT 117

Job #MD1540 DA91

C	Updated as per Council Requirements	NM	08.04.26
B	Updated as per Council Requirements	NM	22.03.26
A	Issue for DA	NM	25.11.25
Issue	Description	By	DATE

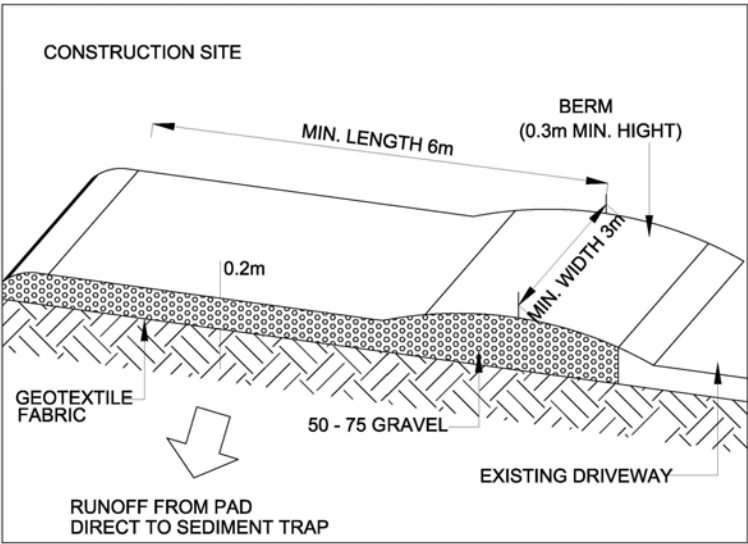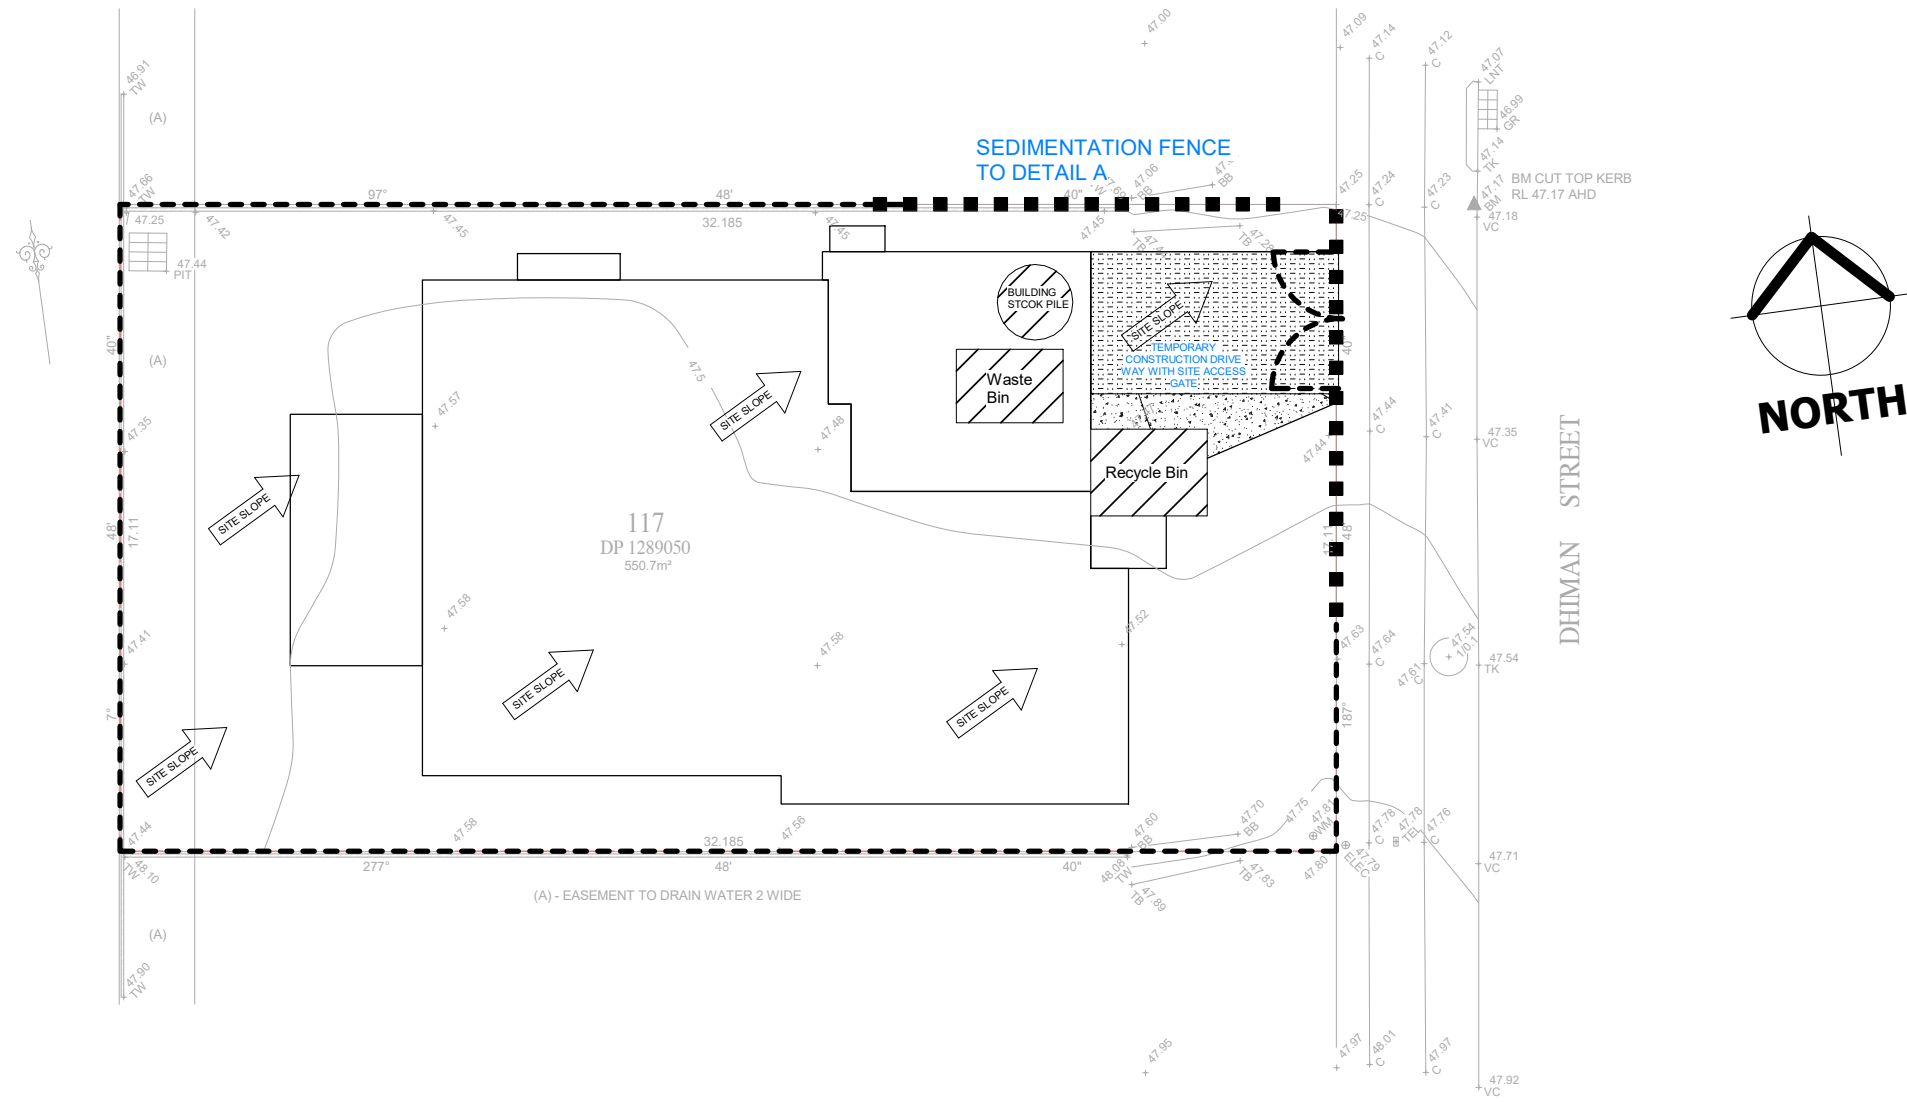


Temporary Construction Driveway
(Not to scale)

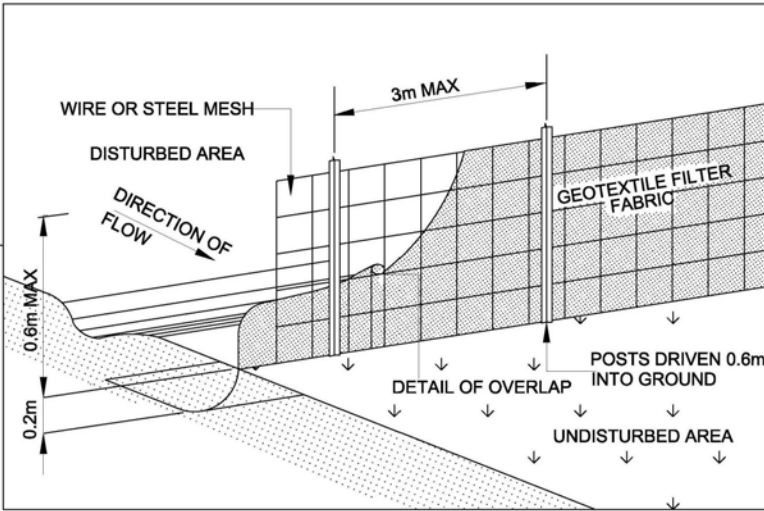

Sediment Fence(not to scale)
Drainage Area 0.6ha Max. Slope Gradient
12 Max. Slope Length 60m Max.

Concept Sedimentation Control Plan

1 : 200

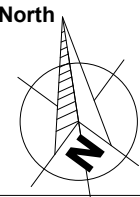

C	Updated as per Council Requirements	NM	08.04.26
B	Updated as per Council Requirements	NM	22.03.26
A	Issue for DA	NM	25.11.25
Issue	Description	By	DATE



EAST ELEVATION
1 : 100



MATERAIL AND FINISHES SCHEDULE		
NUMBER	MATERAIL IMAGE	MATERAIL NAME
1		Render & Paint Colourbond Monument Or Equivalent
2		Render & Paint Dulux Lexicon Or Equivalent
3		Alucobond silver finish
4		Windows/Door Frames Facial/Gutter Woodland Grey Or Equivalent
5		Concrete Driveway Painted in Dulux Domino
6		Garage Door in timber finish as selected
7		Selected metal roof Colorbond Windspray or equivalent
8		AB-Bricks-Expression sBlackstone or Equivalent



MISTRY
DESIGNS

60 Weaver Street
Erskine Park, NSW 2759


m :0430657990
e :nish@nm3d.com.au



Disclaimer:

Do not sclae drawings. Work off figured dimensions. Verify all dimensions on site. Report any discrepancy to the designer.

Design and documentation there of are copyright and remain the property of Mistry Designs and must not be used in anyway, wholly or in part without the written consent of the designer

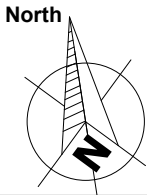

Drawing Title:
Finishes Schedule

Sheet No:
DA.700


Lodged at:	Penrith Council	Scale	As indicated
Drawn by	VT	Date	26JULY2025

PROJECT :
Proposed Dwelling House

Address:
DHIMAN STREET, CLAREMONT MEADOWS
LOT 117


Job #MD1540 DA91

C	Updated as per Council Requirements	NM	08.04.26
B	Updated as per Council Requirements	NM	22.03.26
A	Issue for DA	NM	25.11.25
Issue	Description	By	DATE

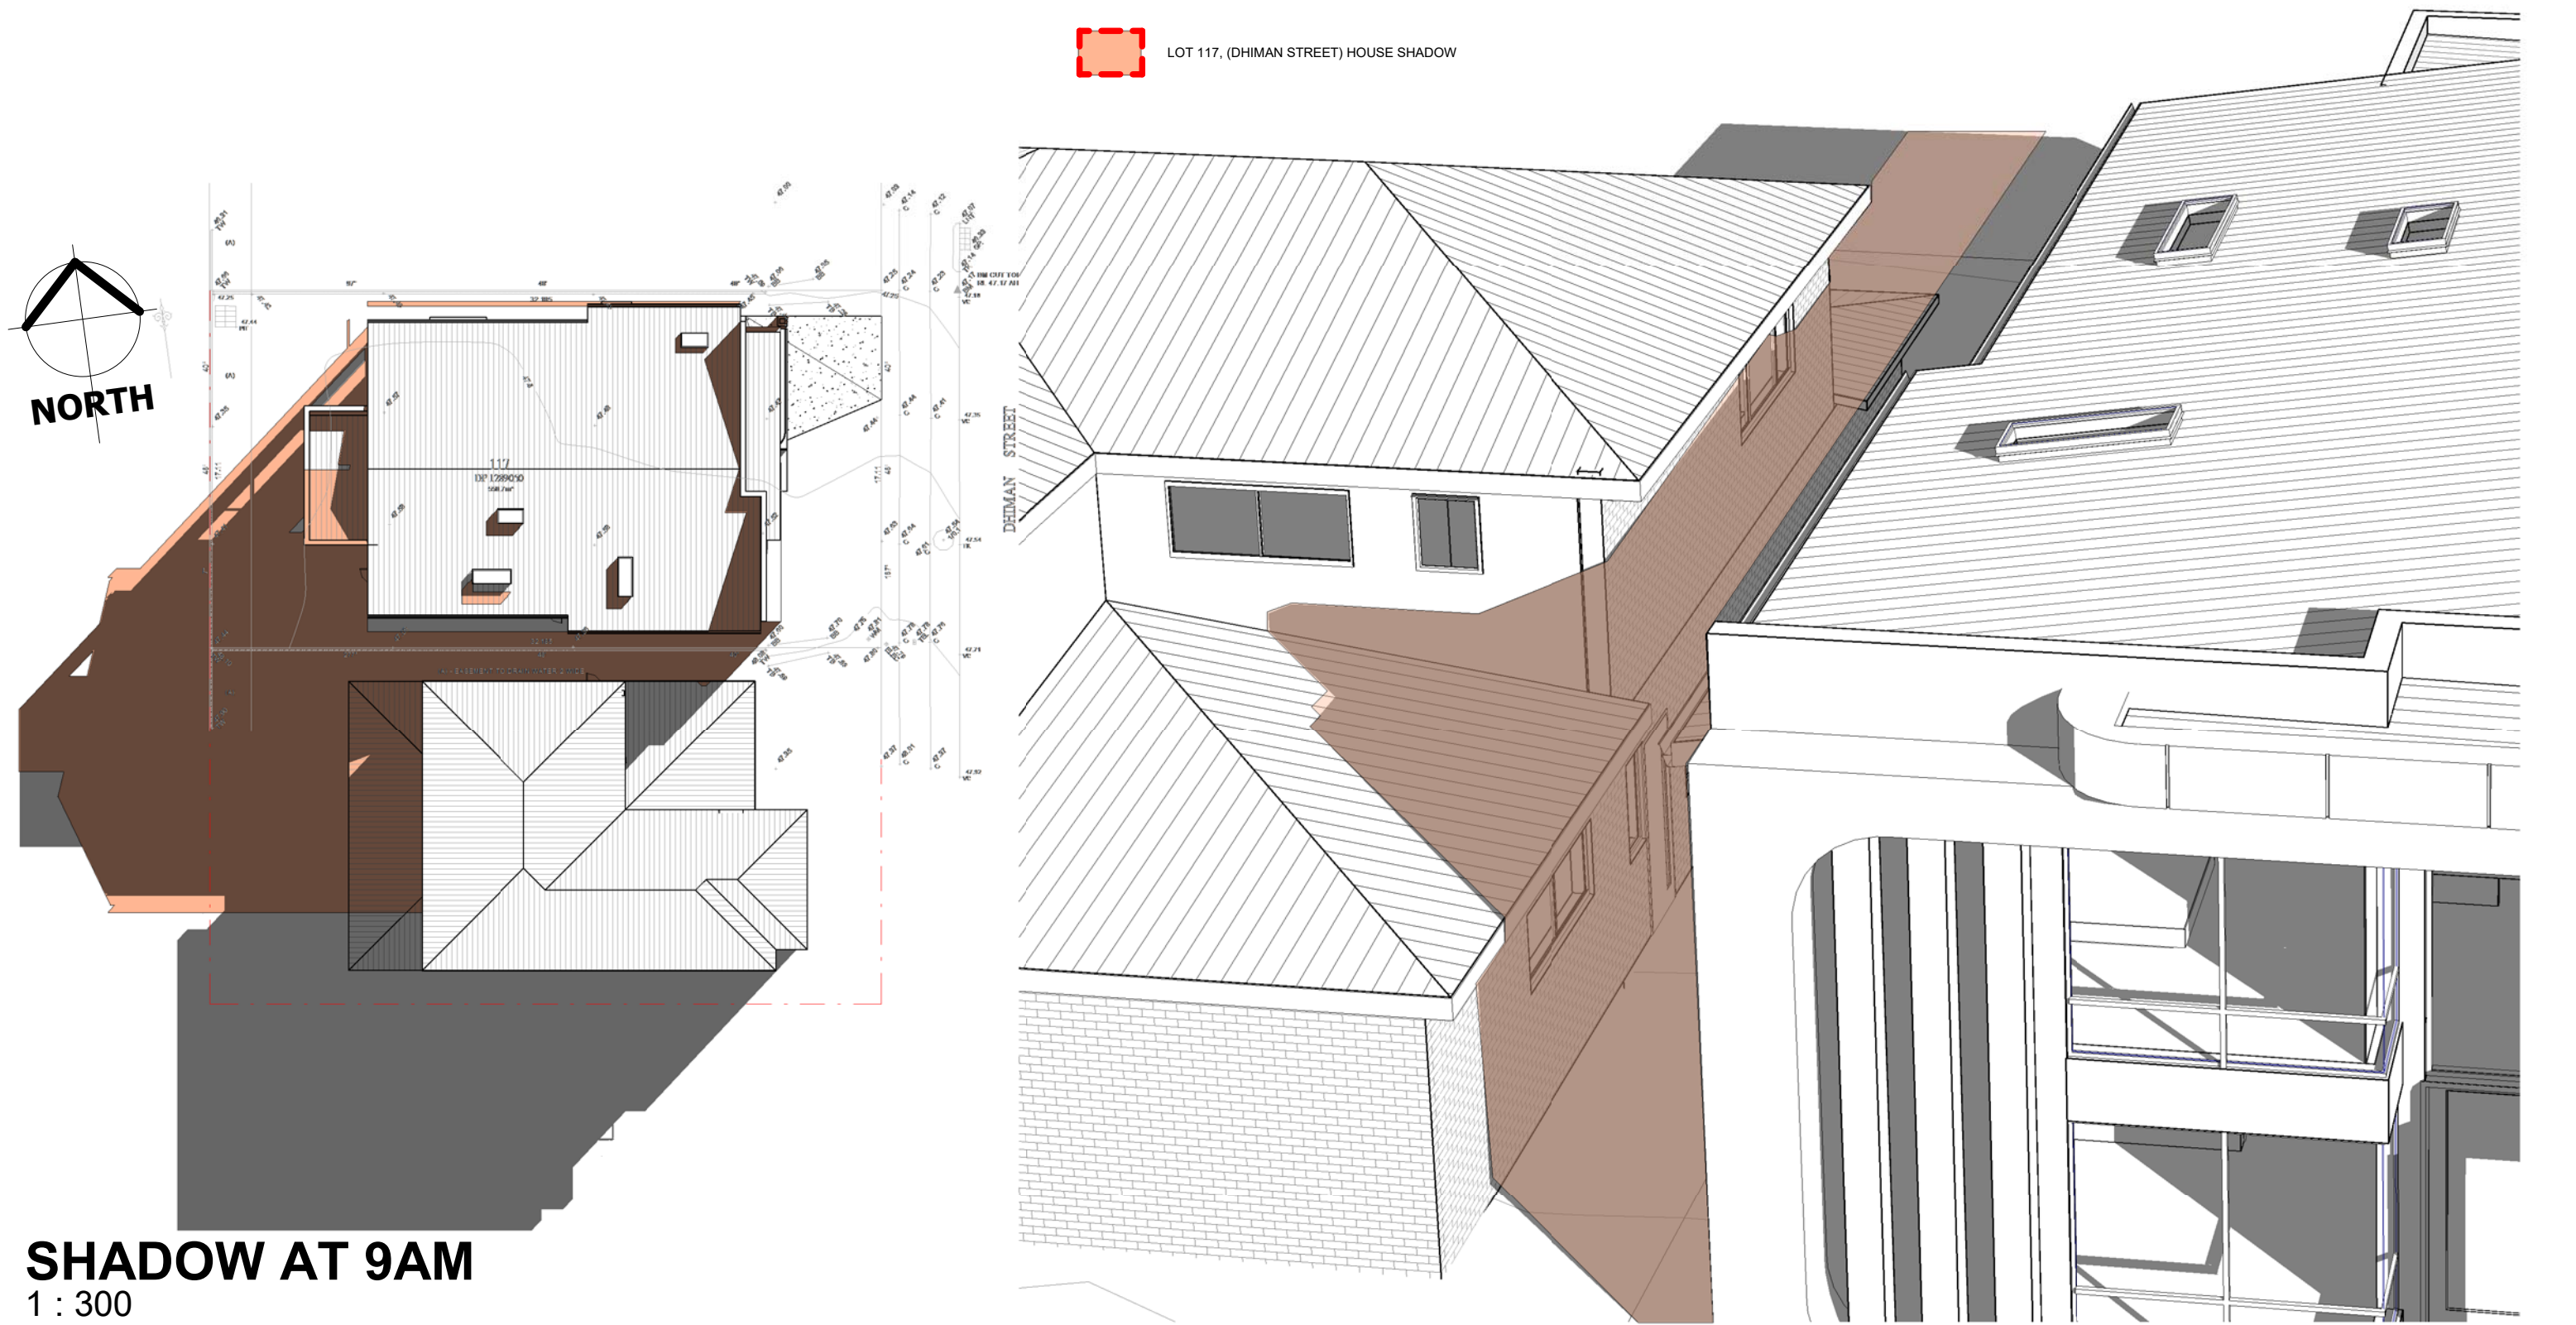


SHADOW AT 9AM
1 : 300
SHADOW DIAGRAM ON 21st OF JUNE

Shadow @ 9AM

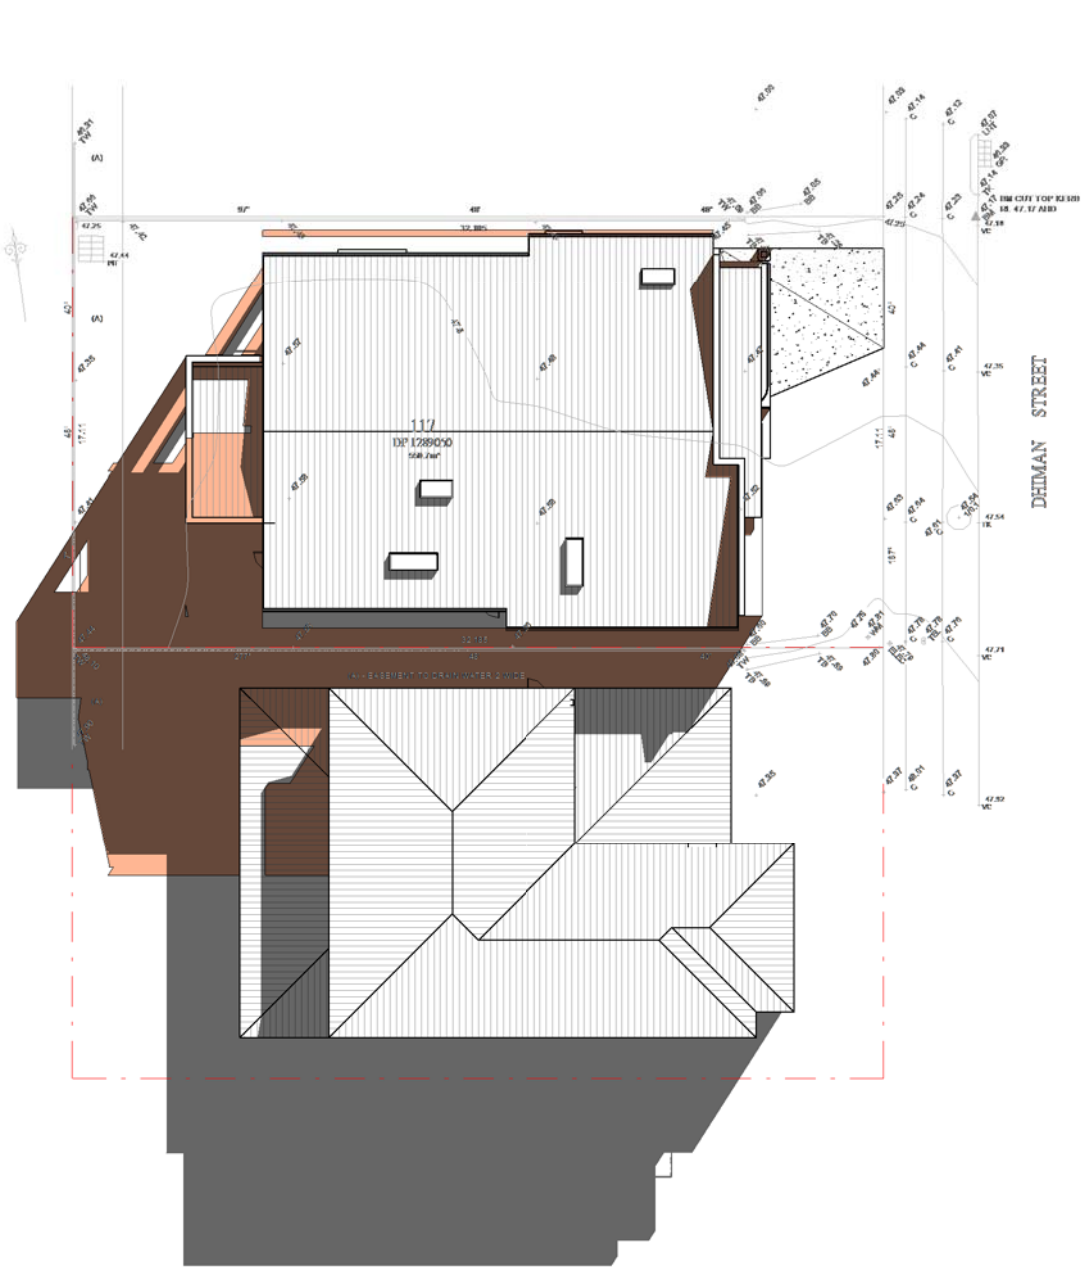

LOT 117, (DHIMAN STREET) HOUSE SHADOW

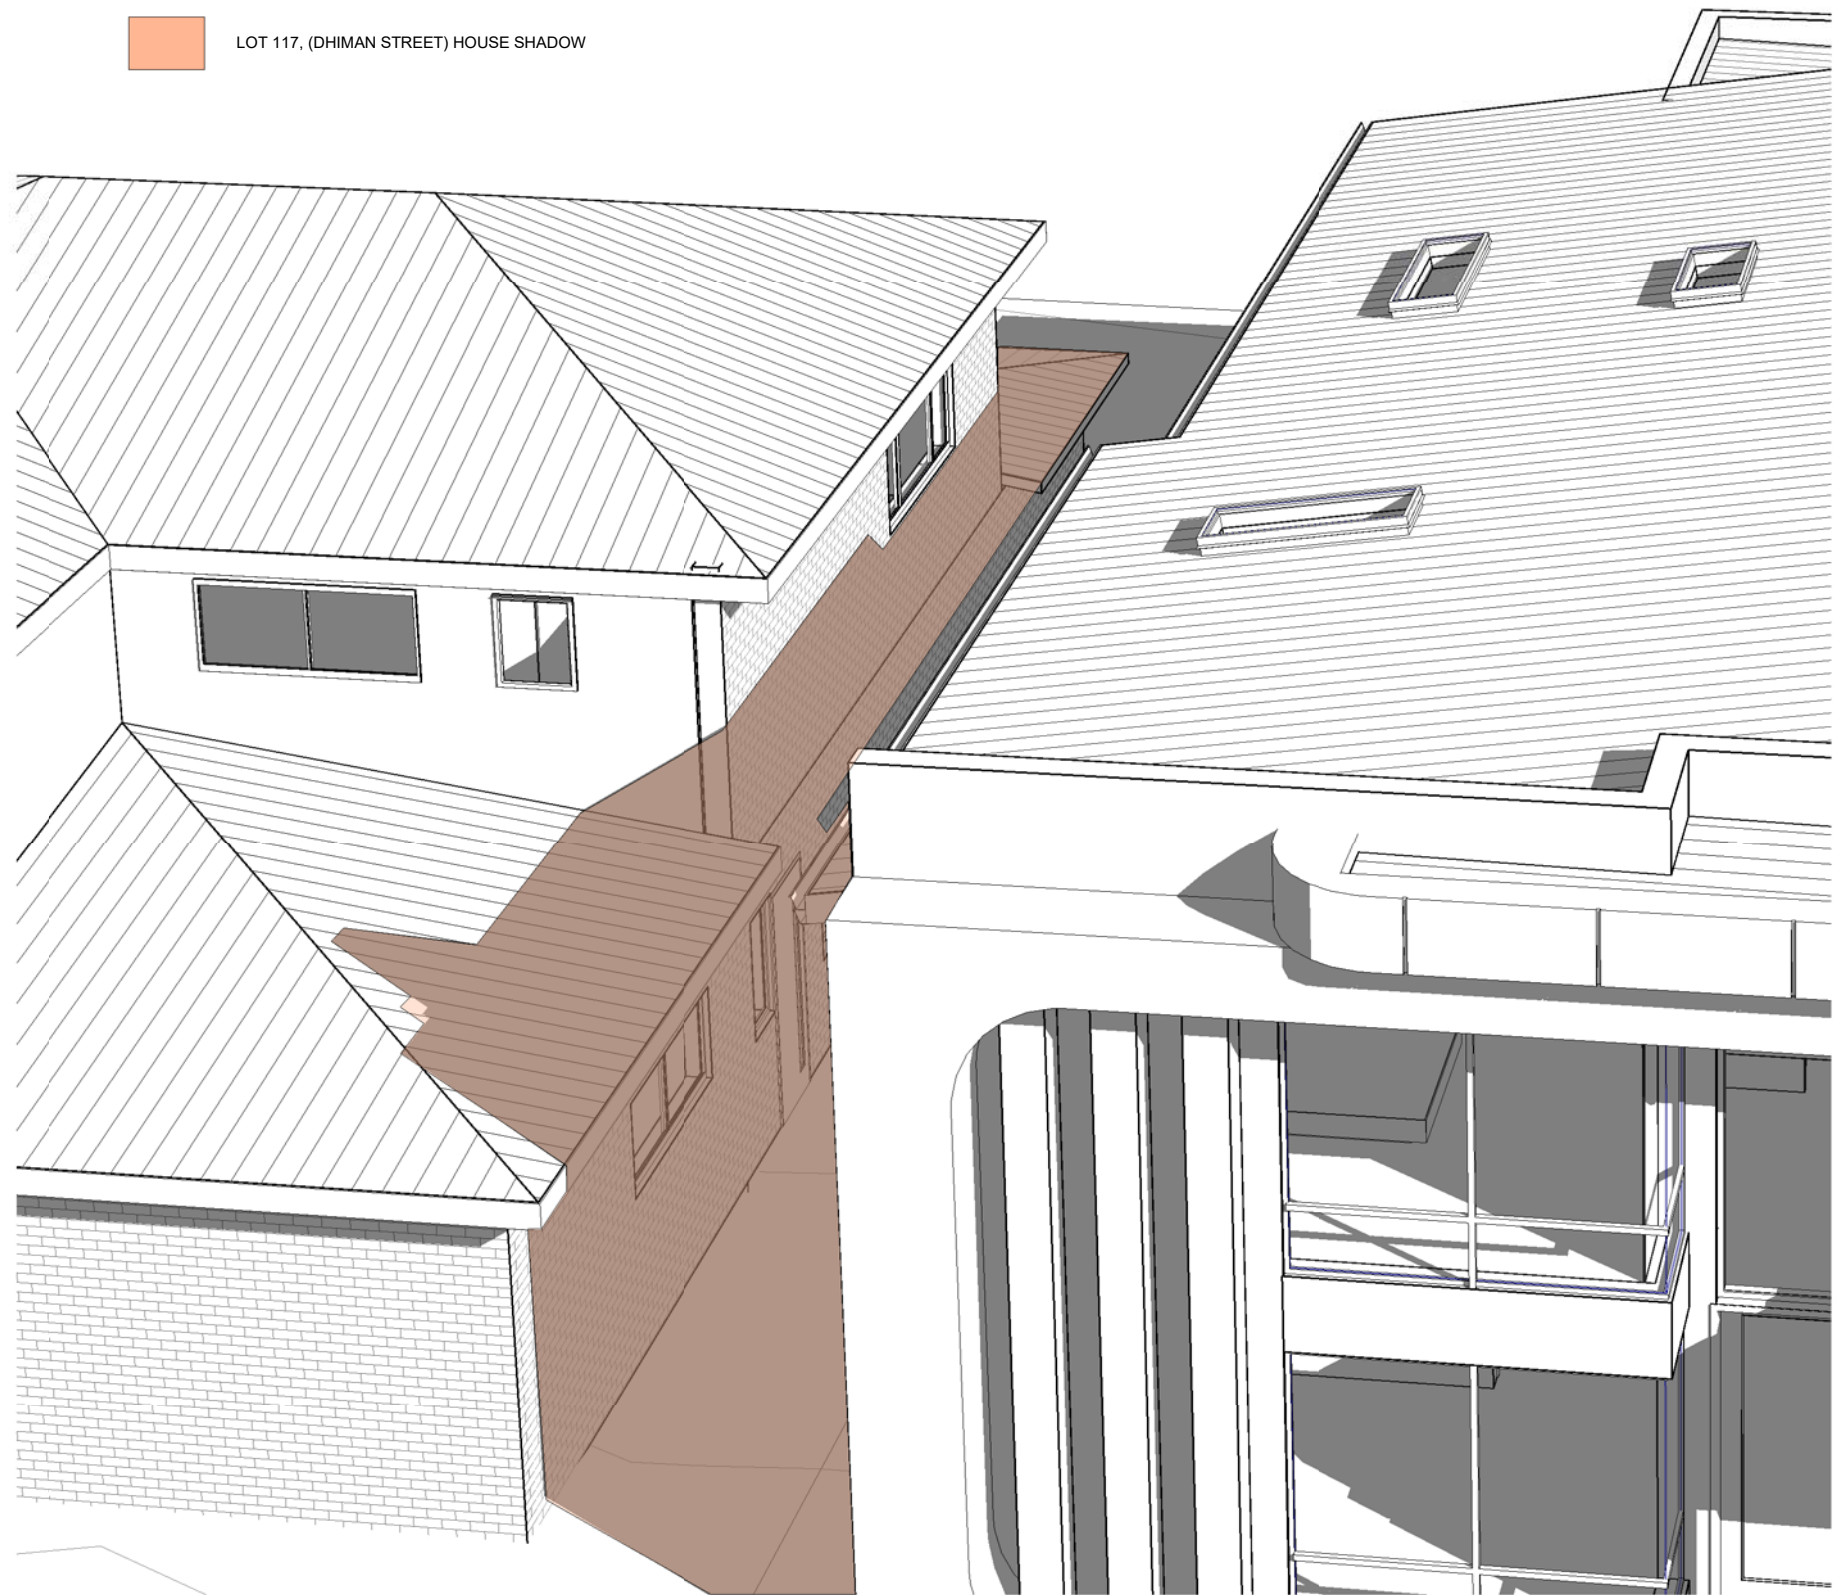

SHADOW AT 10AM
1 : 300

Shadow @ 10AM



**MISTRY
DESIGNS**

60 Weaver Street
Erskine Park, NSW 2759


m :0430657990
e :nish@nm3d.com.au



Disclaimer:

Do not scale drawings. Work off figured dimensions. Verify all dimensions on site. Report any discrepancy to the designer.

Design and documentation there of are copyright and remain the property of Mistry Designs and must not be used in anyway, wholly or in part without the written consent of the designer

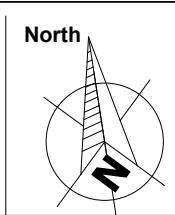


Drawing Title: Shadow Diagram			
Sheet No: DA.601			
Lodged at:	Penrith Council	Scale	As indicated
Drawn by	VT	Date	26JULY2025


PROJECT :
Proposed Dwelling House

Address:
DHIMAN STREET, CLAREMONT MEADOWS
LOT 117

Job #MD1540 DA91			
C	Updated as per Council Requirements	NM	08.04.26
B	Updated as per Council Requirements	NM	22.03.26
A	Issue for DA	NM	25.11.25
Issue	Description	By	DATE

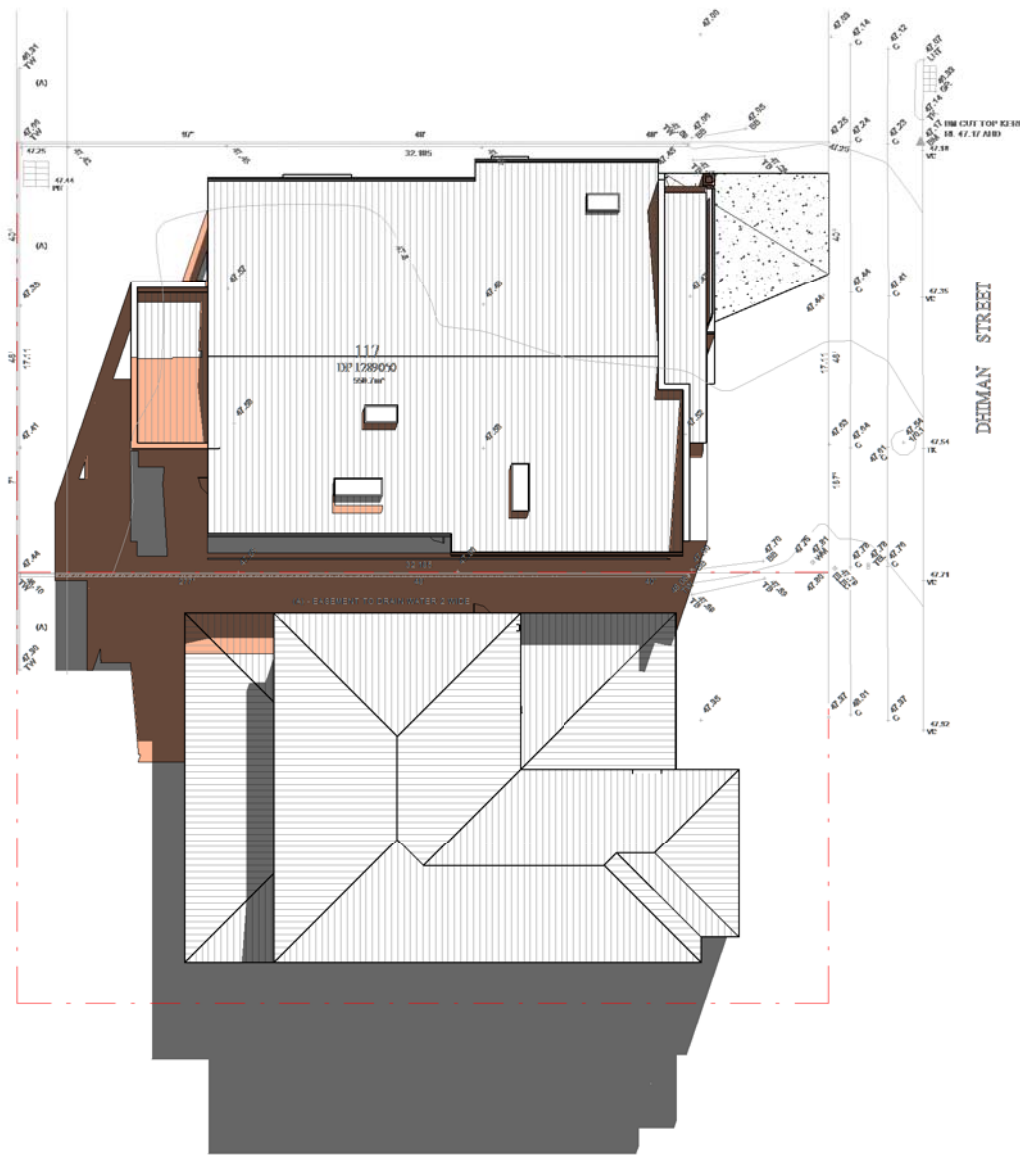

SHADOW AT 11AM
1 : 300

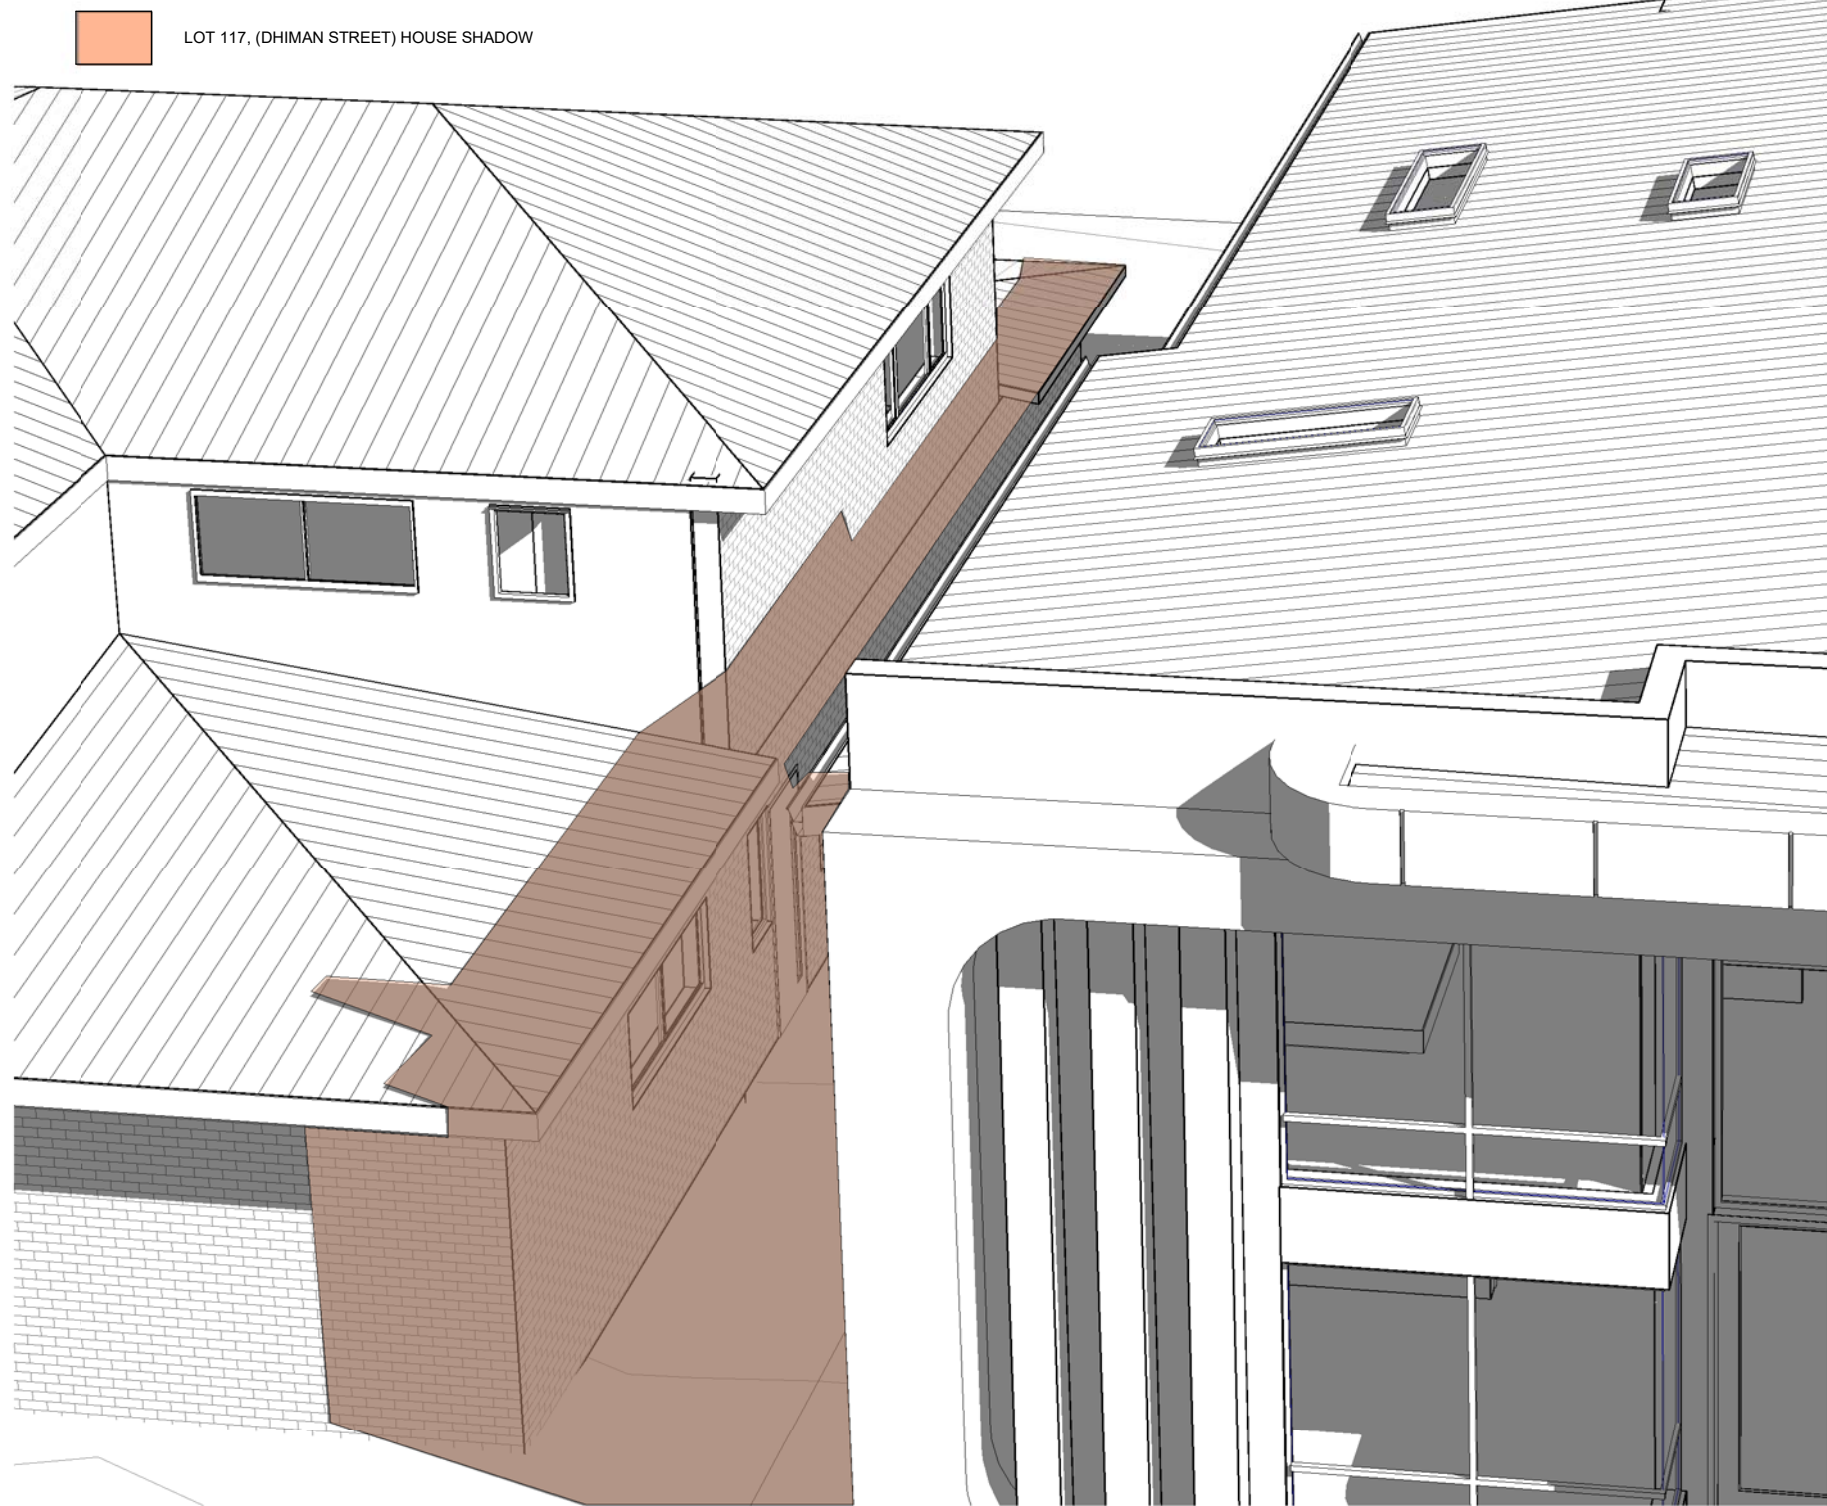

Shadow @ 11AM



MISTRY
DESIGNS

60 Weaver Street
Erskine Park, NSW 2759


m :0430657990
e :nish@nm3d.com.au



Disclaimer:

Do not scale drawings. Work off figured dimensions. Verify all dimensions on site. Report any discrepancy to the designer.

Design and documentation there of are copyright and remain the property of Mistry Designs and must not be used in anyway, wholly or in part without the written consent of the designer

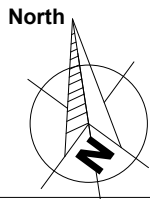

Drawing Title:
Shadow Diagram

Sheet No:
DA.602


Lodged at:	Penrith Council	Scale	As indicated
Drawn by	VT	Date	26JULY2025

PROJECT :
Proposed Dwelling House

Address:
DHIMAN STREET, CLAREMONT MEADOWS
LOT 117

Job #MD1540 DA91

C	Updated as per Council Requirements	NM	08.04.26
B	Updated as per Council Requirements	NM	22.03.26
A	Issue for DA	NM	25.11.25
Issue	Description	By	DATE

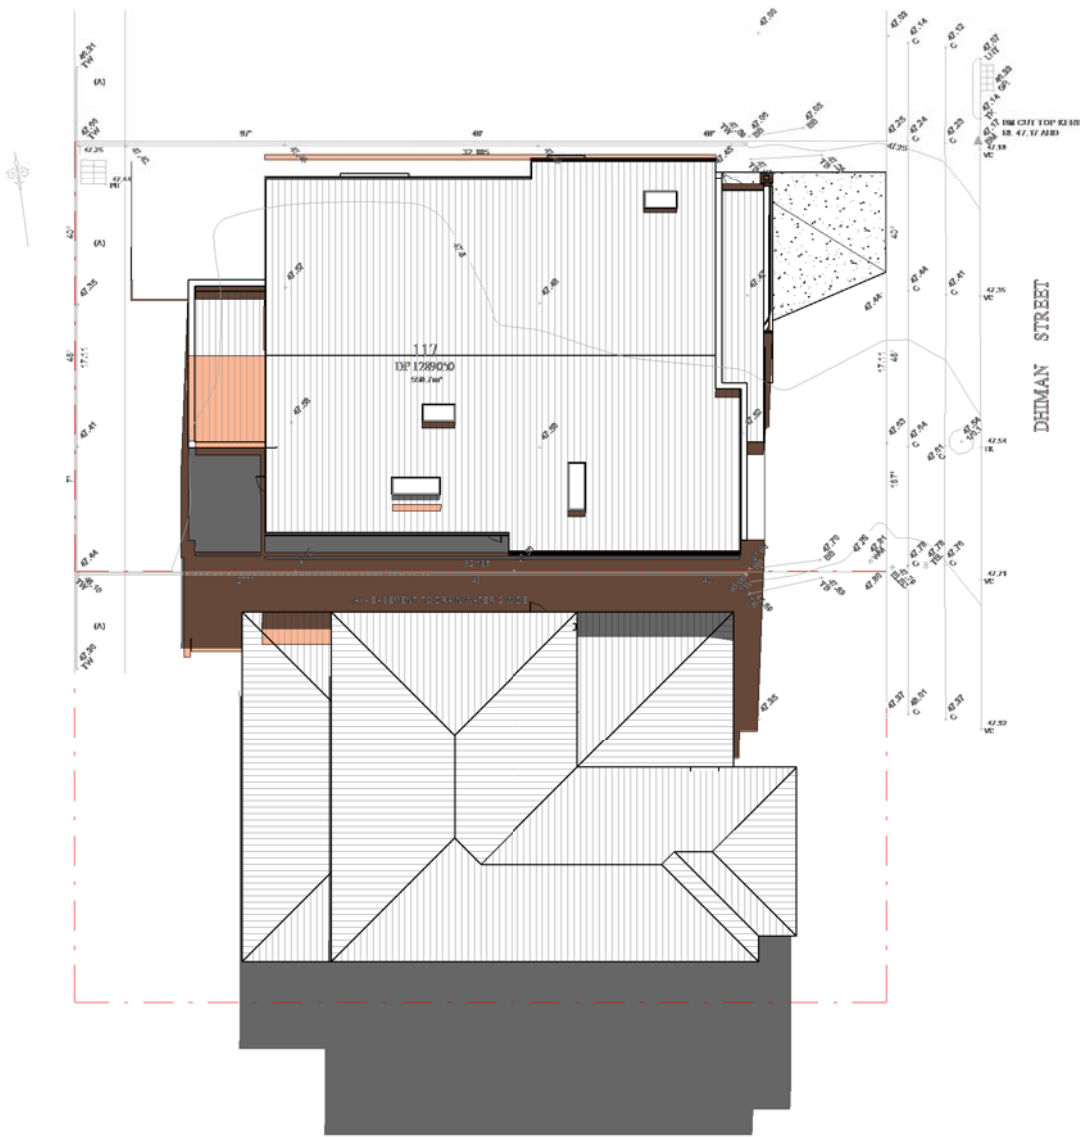

LOT 117, (DHIMAN STREET) HOUSE SHADOW



SHADOW AT 12PM
1 : 300

Shadow @ 12PM



**MISTRY
DESIGNS**

60 Weaver Street
Erskine Park, NSW 2759

m :0430657990
e :nish@nm3d.com.au



Disclaimer:

Do not scale drawings. Work off figured dimensions. Verify all dimensions on site. Report any discrepancy to the designer.

Design and documentation there of are copyright and remain the property of Mistry Designs and must not be used in anyway, wholly or in part without the written consent of the designer



Drawing Title:
Shadow Diagram

Sheet No:
DA.603

Lodged at:	Penrith Council	Scale	As indicated
Drawn by	VT	Date	26JULY2025


PROJECT :
Proposed Dwelling House

Address:
DHIMAN STREET, CLAREMONT MEADOWS
LOT 117

Job #MD1540 DA91

C	Updated as per Council Requirements	NM	08.04.26
B	Updated as per Council Requirements	NM	22.03.26
A	Issue for DA	NM	25.11.25
Issue	Description	By	DATE

LOT 117, (DHIMAN STREET) HOUSE SHADOW

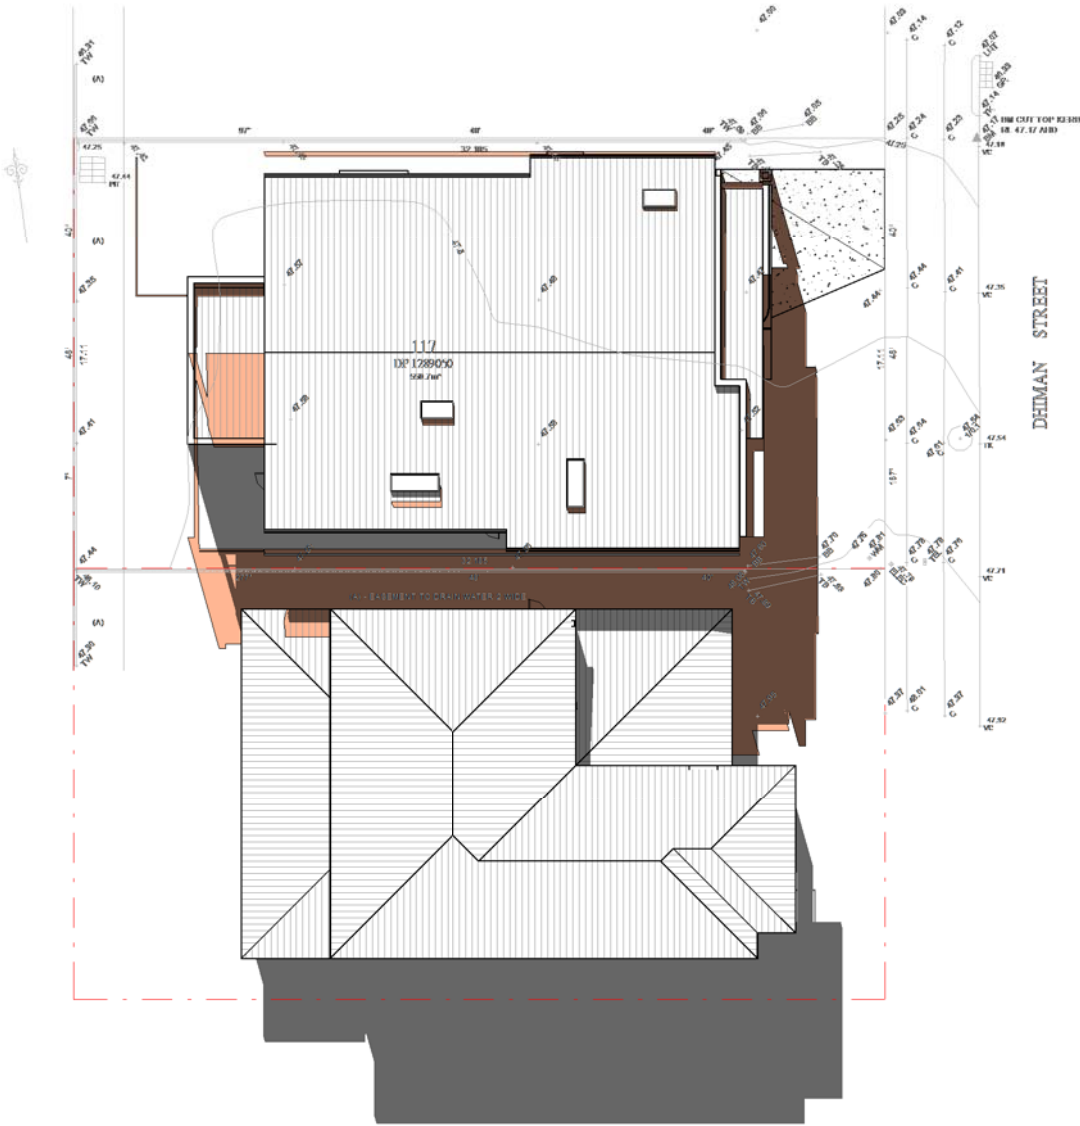

SHADOW AT 1PM
1 : 300

Shadow @ 1PM



**MISTRY
DESIGNS**

60 Weaver Street
Erskine Park, NSW 2759

m :0430657990
e :nish@nm3d.com.au




1100.com.au

Disclaimer:

Do not scale drawings. Work off figured dimensions. Verify all dimensions on site. Report any discrepancy to the designer.

Design and documentation there of are copyright and remain the property of Mistry Designs and must not be used in anyway, wholly or in part without the written consent of the designer

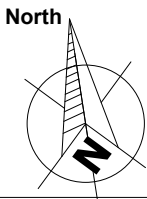


Drawing Title: Shadow Diagram			
Sheet No: DA.604			
Lodged at:	Penrith Council	Scale	As indicated
Drawn by	VT	Date	26JULY2025

PROJECT :
Proposed Dwelling House

Address:
DHIMAN STREET, CLAREMONT MEADOWS
LOT 117

Job #MD1540 DA91			
C	Updated as per Council Requirements	NM	08.04.26
B	Updated as per Council Requirements	NM	22.03.26
A	Issue for DA	NM	25.11.25
Issue	Description	By	DATE

LOT 117, (DHIMAN STREET) HOUSE SHADOW

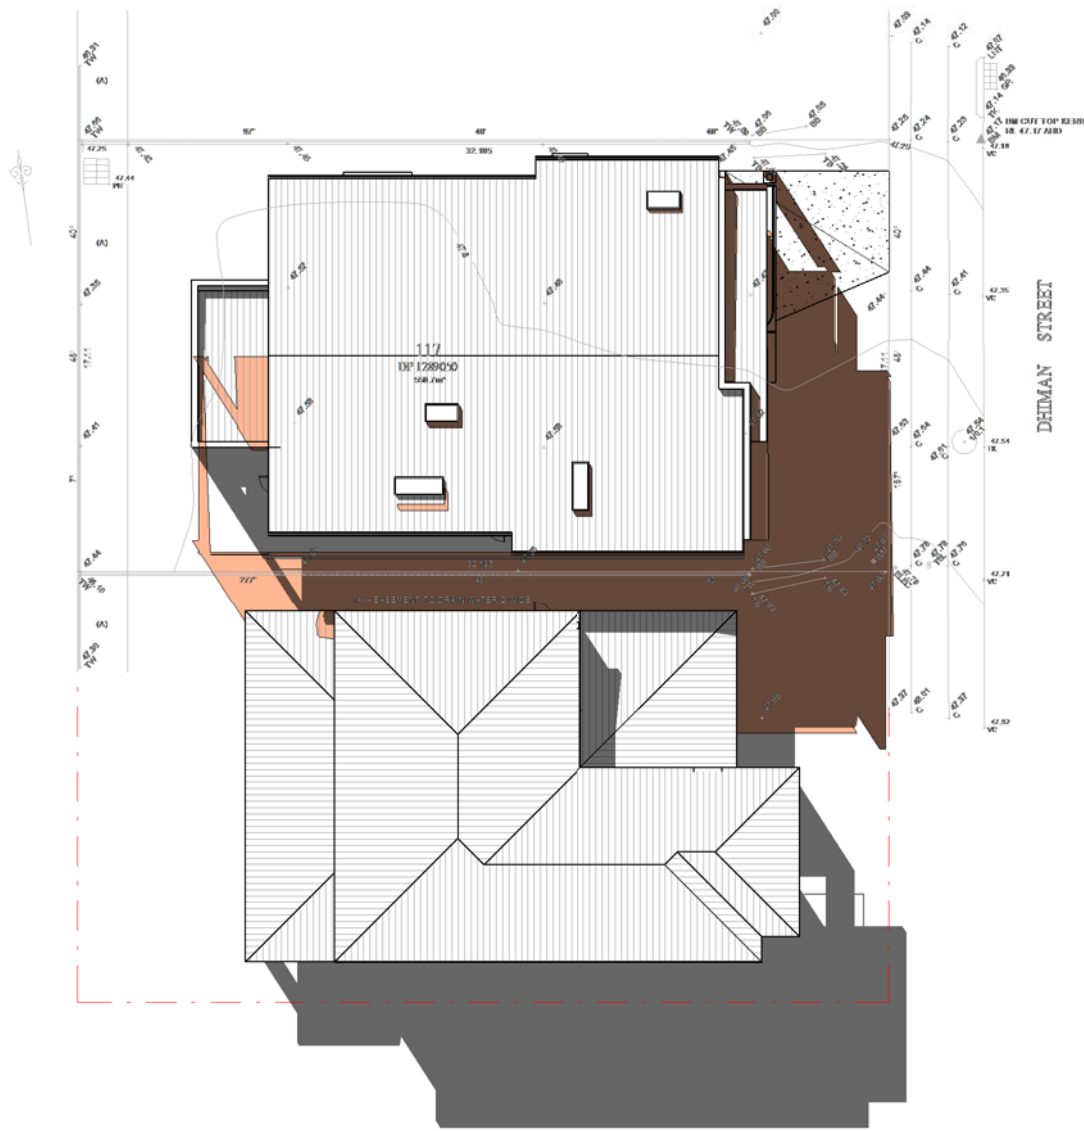

SHADOW AT 2PM
1 : 300



Shadow @ 2PM



MISTRY
DESIGNS

60 Weaver Street
Erskine Park, NSW 2759


m :0430657990
e :nish@nm3d.com.au



Disclaimer:

Do not scale drawings. Work off figured dimensions. Verify all dimensions on site. Report any discrepancy to the designer.

Design and documentation there of are copyright and remain the property of Mistry Designs and must not be used in anyway, wholly or in part without the written consent of the designer

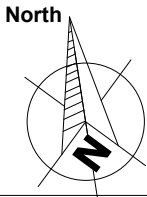

Drawing Title:
Shadow Diagram

Sheet No:
DA.605


Lodged at:	Penrith Council	Scale	As indicated
Drawn by	VT	Date	26JULY2025

PROJECT :
Proposed Dwelling House


Address:
DHIMAN STREET, CLAREMONT MEADOWS
LOT 117

Job #MD1540 DA91

C	Updated as per Council Requirements	NM	08.04.26
B	Updated as per Council Requirements	NM	22.03.26
A	Issue for DA	NM	25.11.25
Issue	Description	By	DATE

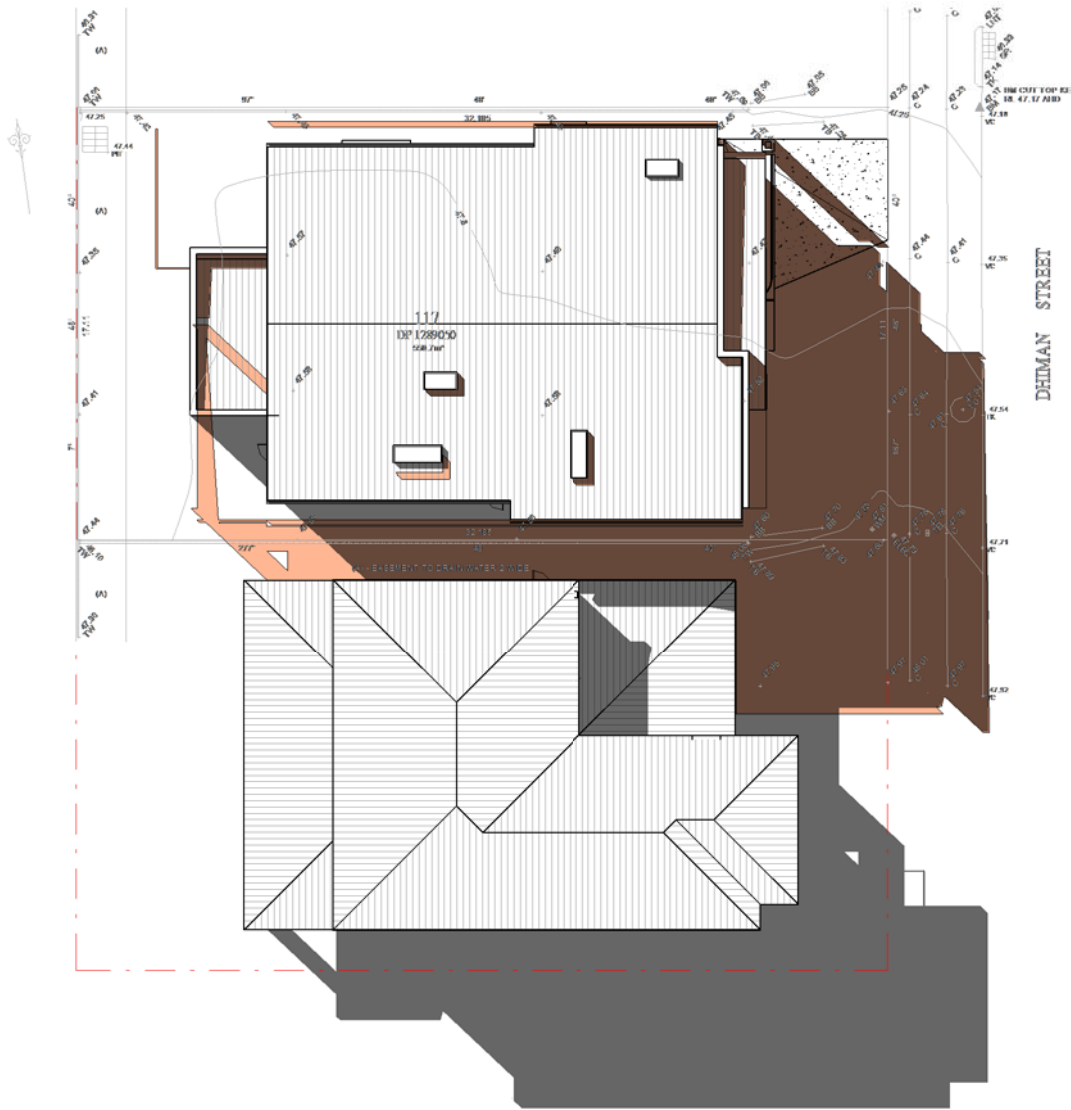

LOT 117, (DHIMAN STREET) HOUSE SHADOW

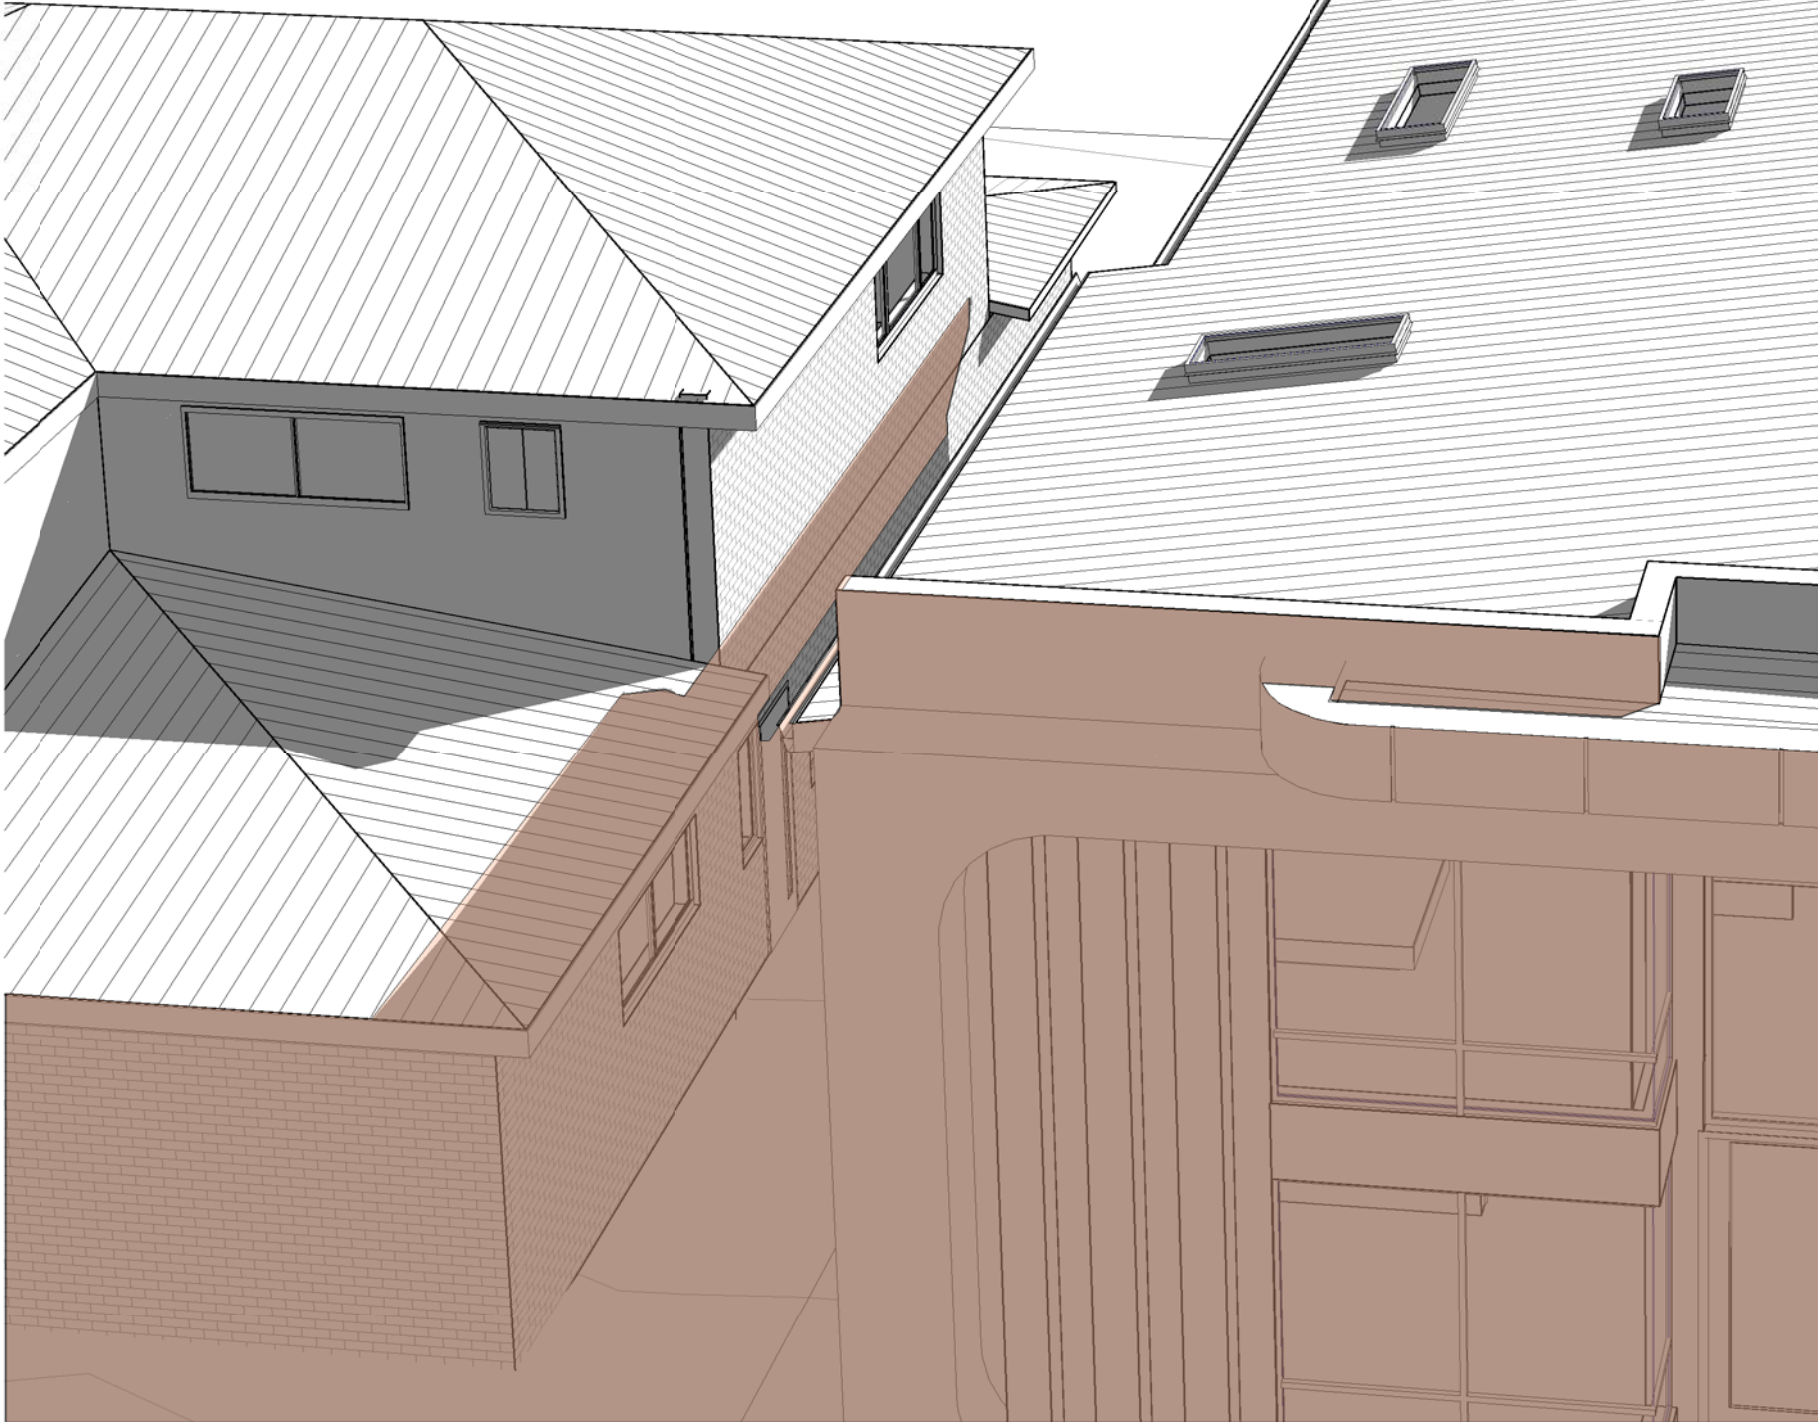

SHADOW AT 3PM
1 : 300

Shadow @ 3PM



MISTRY
DESIGNS

60 Weaver Street
Erskine Park, NSW 2759


m :0430657990
e :nish@nm3d.com.au



Disclaimer:

Do not scale drawings. Work off figured dimensions. Verify all dimensions on site. Report any discrepancy to the designer.

Design and documentation there of are copyright and remain the property of Mistry Designs and must not be used in anyway, wholly or in part without the written consent of the designer

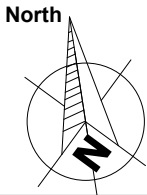

Drawing Title:
Shadow Diagram

Sheet No:
DA.606

Lodged at:	Penrith Council	Scale	As indicated
Drawn by	VT	Date	26JULY2025

PROJECT :
Proposed Dwelling House

Address:
DHIMAN STREET, CLAREMONT MEADOWS
LOT 117

Job #MD1540 DA91

C	Updated as per Council Requirements	NM	08.04.26
B	Updated as per Council Requirements	NM	22.03.26
A	Issue for DA	NM	25.11.25
Issue	Description	By	DATE