

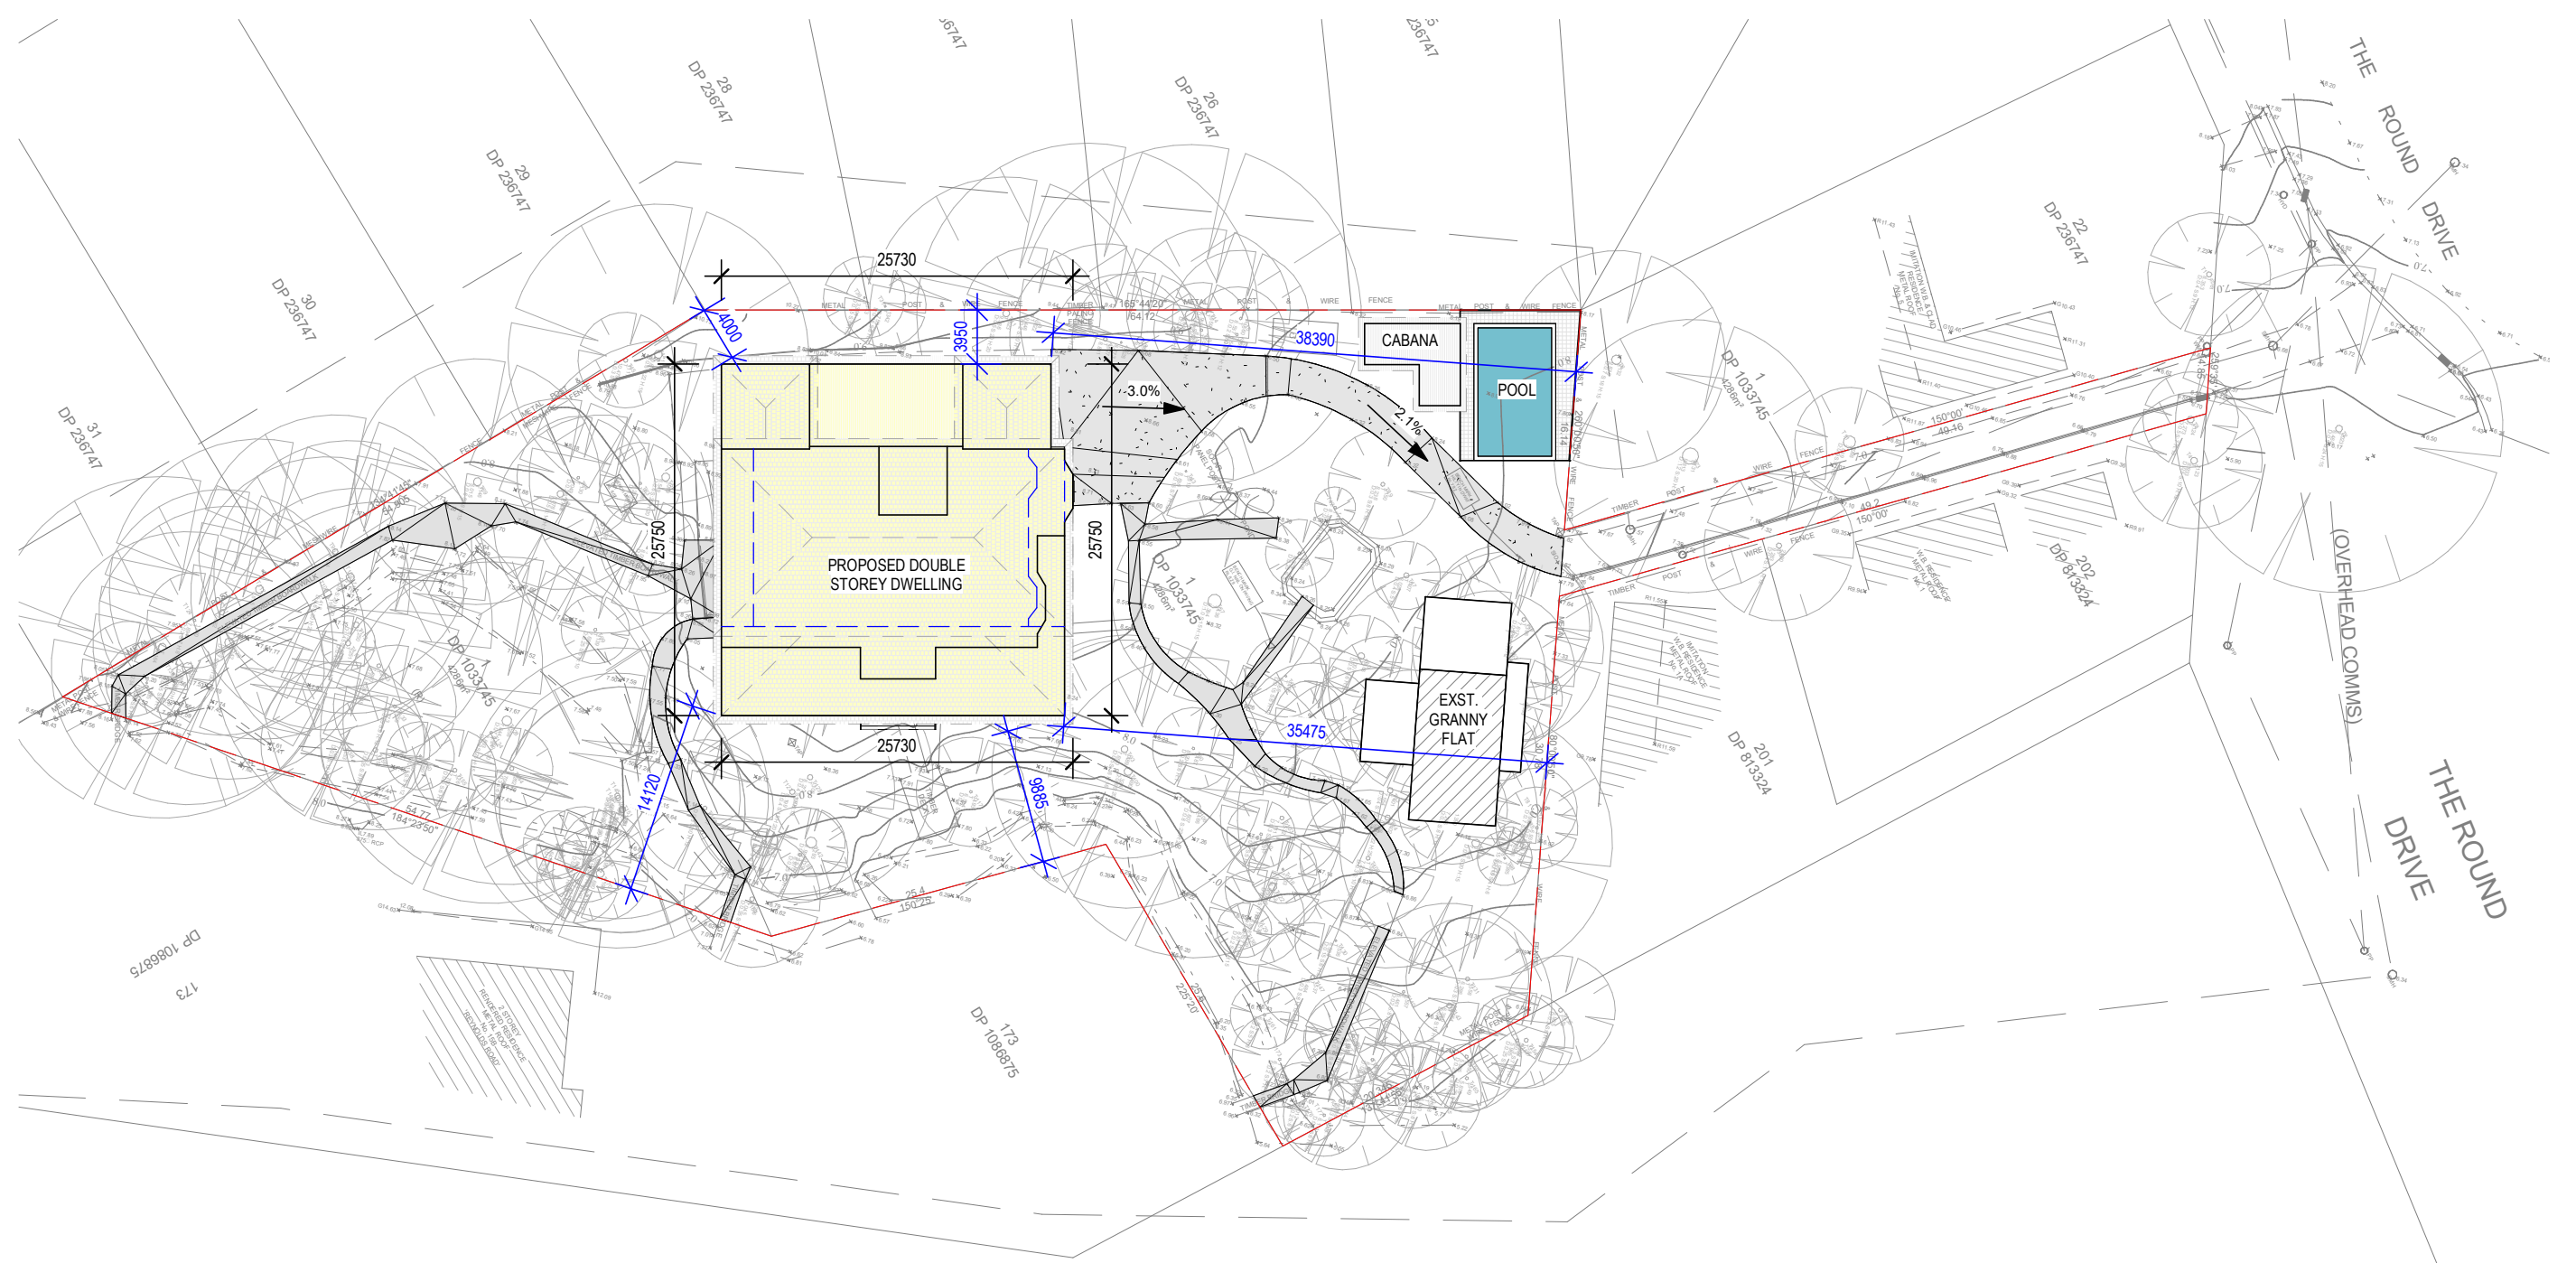


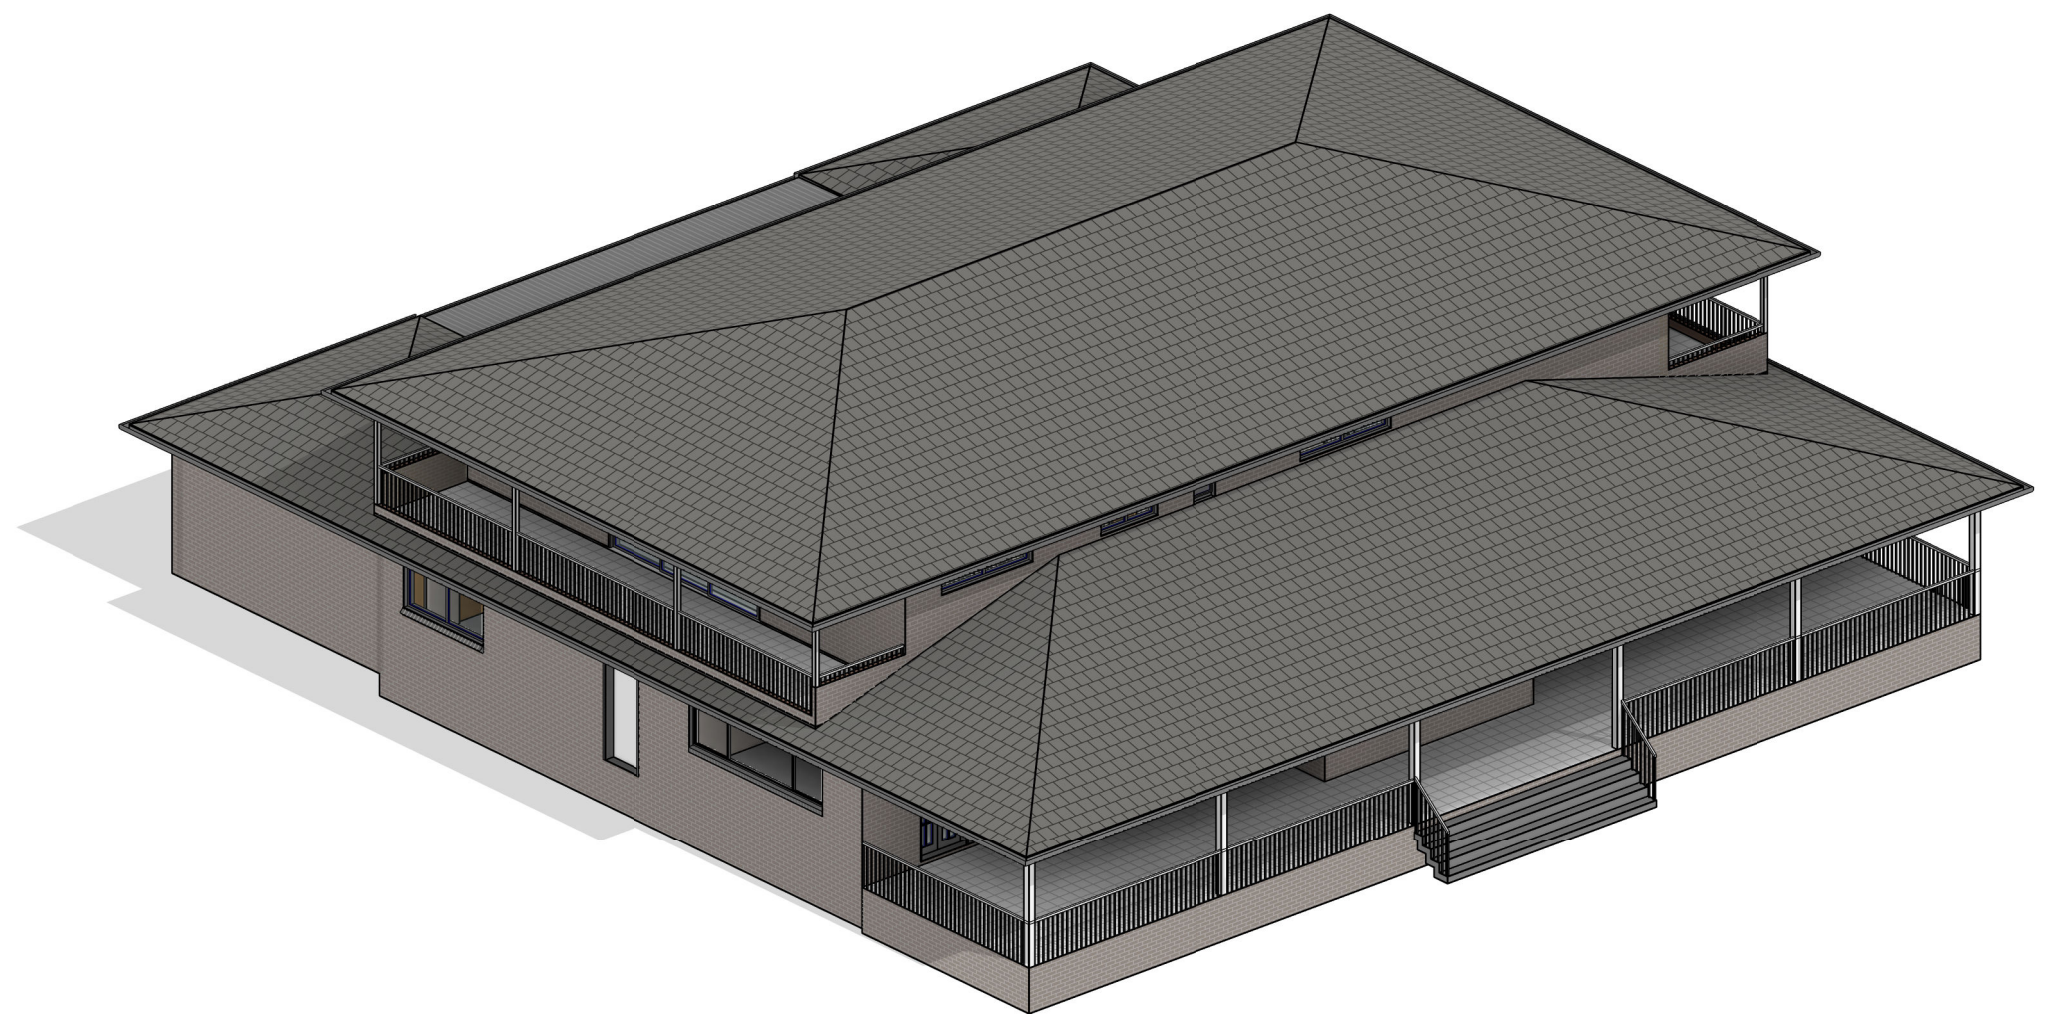

③ SITE LOCATION PLAN

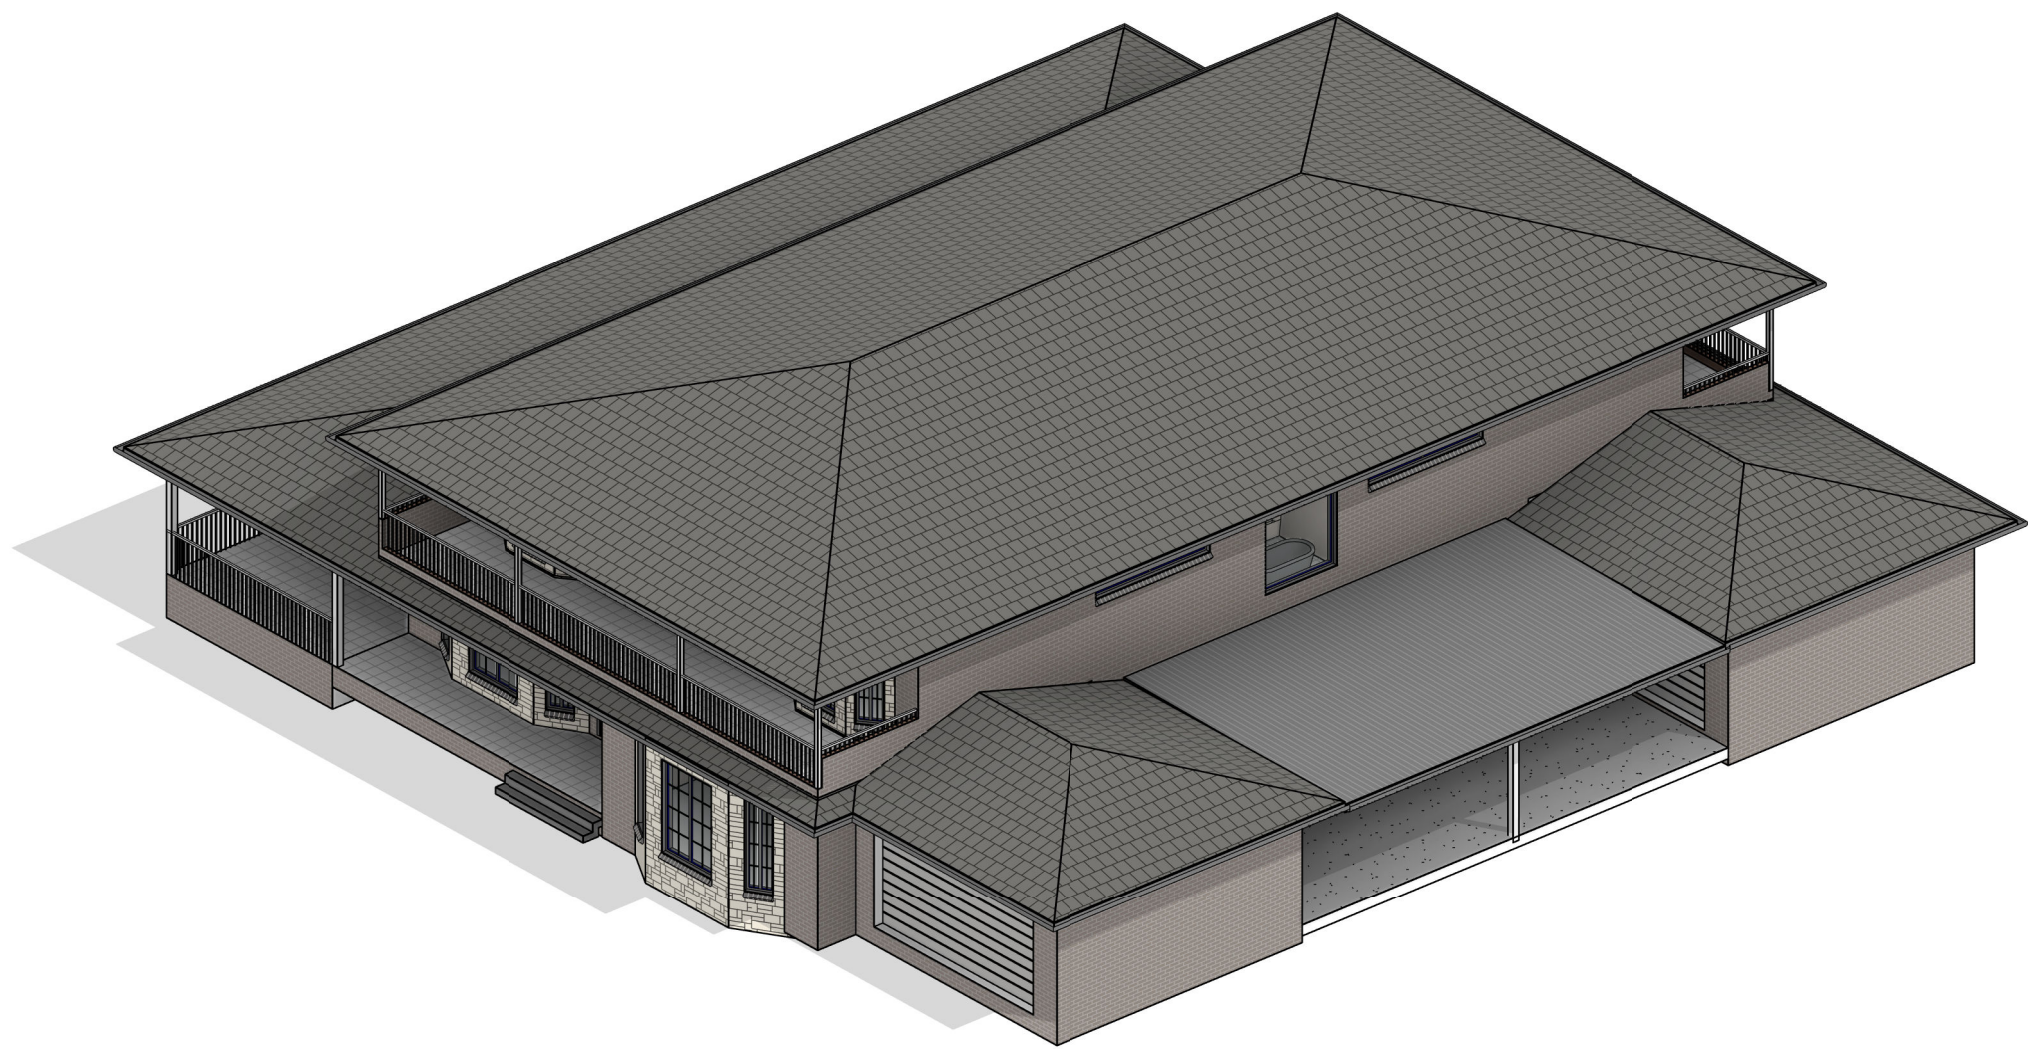

- REFER TO BCA REPORT FOR BUILDING REQUIREMENTS / PERFORMANCE SOLUTION / BUILDING UPGRADE.
- REFER TO FER REPORT PREPARED BY FE CONSULTING P/L FOR PERFORMANCE SOLUTION / CONSTRUCTION UPGRADE.
- SITE AFFECTED BY BUSHFIRE PRONE. BAL 12.5 RATED MATERIALS MUST BE USED TO COMPLY WITH THE BUSHFIRE ASSESSMENT REPORT.

- BUILDERS' WORK TO COMPLY WITH THE LATEST BCA AND ITS AMENDMENTS AND RELEVANT AUSTRALIAN STANDARDS REFERRED WITHIN.

No.	Description	Date
1	REVISE AS PER COUNCIL REQUIREMENTS	22/03/2025



CLIENT & PROJECT: LOT 1 IN DP 1033745
**CONSTRUCTION CERTIFICATE FOR DOUBLE STOREY DWELLING
 AT NO.3 GILL AVENUE, AVOCA BEACH, NSW 2251**

CONSTRUCTION CERTIFICATE

DATE: 22/03/2025

DWG NO: CC-01



DRW BY: LT

SCALE: As indicated (A2)

NOTES:

1. CHECK DIMENSIONS ON SITE BEFORE PROCEEDING WITH THE WORK OF THE CONTRACT. NOTIFY BUILDING DESIGNER OF OMISSIONS OR CONFLICT IN DRAWINGS OR SPECIFICATIONS.

2. FIGURED DIMENSIONS ARE TO BE TAKEN IN PREFERENCE TO SCALE. DO NOT SCALE OFF DRAWINGS.


3. ALL CONSTRUCTION WORK IS TO COMPLY WITH RELEVANT AUSTRALIAN STANDARDS AND THE NCC.

4. REFER TO ACCOMPANYING BASIX CERTIFICATE REFERENCED FOR COMMITMENTS FOR THIS DEVELOPMENT.

5.SA: SMOKE ALARM
SMOKE ALARMS TO BE INSTALLED IN ACCORDANCE WITH AS 3786-2014 & CONNECTED TO MAINS POWER

SITE CALCULATIONS	
SITE AREA: 4286 sqm	
PROPOSED GROUND FLOOR	358 sqm
PROPOSED GARAGE	36 sqm
PROPOSED FIRST FLOOR	213 sqm
PROPOSED POOL CABANA	30 sqm
EXISTING GRANNY FLAT	60 sqm
TOTAL FLOOR AREA	661 sqm (15.4%)
SITE COVERAGE (MAX 30%)	553.1 sqm (12.9%)
PRIVATE OPEN SPACE	50 sqm
LANDSCAPE AREA (MIN 60%)	2633.7 sqm (61.4%)

LOT 1 IN DP 1033745
CONSTRUCTION CERTIFICATE FOR DOUBLE STOREY DWELLING
AT NO.3 GILL AVENUE, AVOCA BEACH, NSW 2251

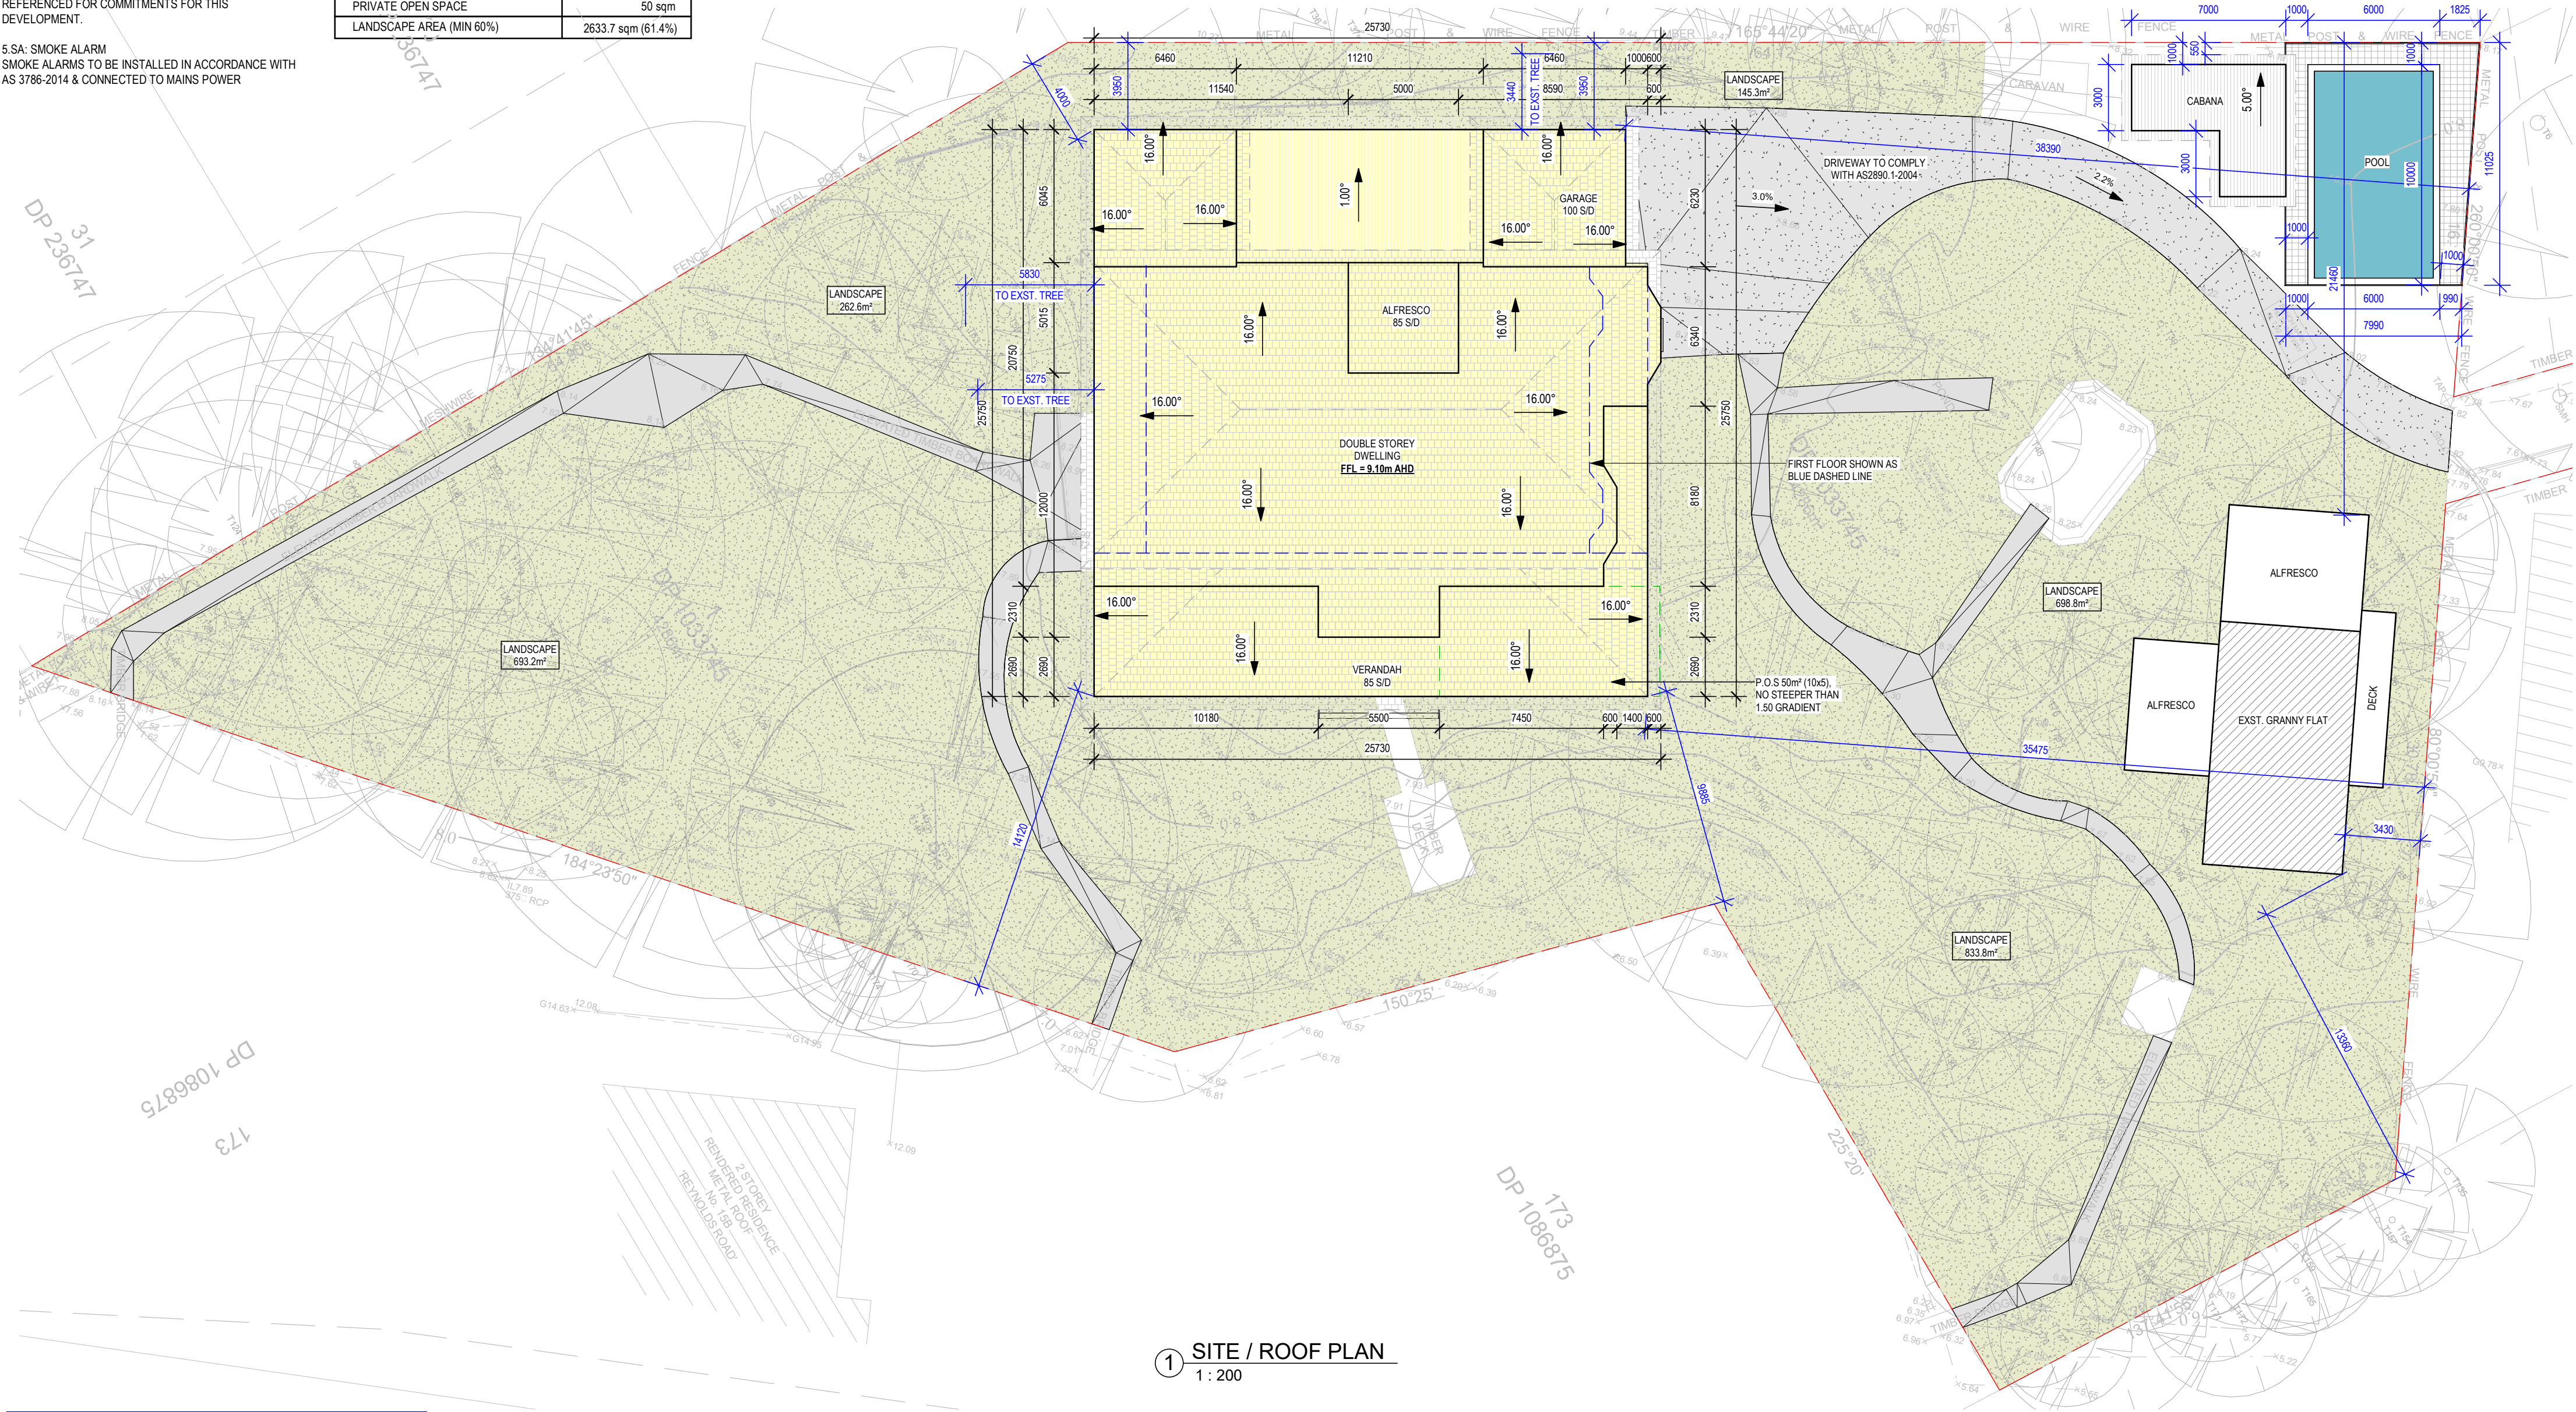

1 SITE / ROOF PLAN
1: 200

IMPORTANT CONSTRUCTION NOTES:

- REFER TO BCA REPORT FOR BUILDING REQUIREMENTS / PERFORMANCE SOLUTION / BUILDING UPGRADE.
- REFER TO FER REPORT PREAPRED BY FE CONSULTING P/L FOR PERFORMANCE SOLUTION / CONSTRUCTION UPGRADE.
- SITE AFFECTED BY BUSHFIRE PRONE. BAL 12.5 RATED MATERIALS MUST BE USED TO COMPLY WITH THE BUSHFIRE ASSESSMENT REPORT.

© THIS DRAWING IS THE PROPERTY OF LT DESIGN & CONSULTING PTY LTD AND WE RESERVE THE COPYRIGHT TO ALL OUR DESIGNS WHICH CANNOT BE REPRODUCED (IN PART OR IN WHOLE) BEFORE FIRST OBTAINING WRITTEN CONSENT. CONTRAVENTION WILL BE PROSECUTED

- FIGURED DIMENSIONS TO BE TAKEN IN PREFERENCE TO SCALE.

- BUILDERS' WORK TO COMPLY WITH THE LATEST BCA AND ITS AMENDMENTS AND RELEVANT AUSTRALIAN STANDARDS REFERRED WITHIN.

No.	Description	Date
1	REVISE AS PER COUNCIL REQUIREMENTS	22/03/2025



Building Design | 3D Modeling | Drafting | Detailing



BUILDING DESIGNERS AUSTRALIA
Accreditation No: 6302
Shop 6A/80 Thorneby Rd, Fairfield West
0414 891 998 - Le@LTDesign.net.au

DRAWING:
SITE / ROOF PLAN

CLIENT & PROJECT: LOT 1 IN DP 1033745
CONSTRUCTION CERTIFICATE FOR DOUBLE STOREY DWELLING
AT NO.3 GILL AVENUE, AVOCA BEACH, NSW 2251

CONSTRUCTION CERTIFICATE

DATE:
22/03/2025
DWG NO:
CC-02



DRW BY:
LT

SCALE: As indicated (A2)

SITE MANAGEMENT PLAN / DEMOLITION PLAN /
GENERAL CONSTRUCTION NOTES

PROVIDE 1800mm HIGH SAFETY & SECURITY FENCE FOR THE DURATION OF THE DEMOLITION & CONSTRUCTION WORKS. SILT FENCE, GEOTEXTILE FABRIC OR THE EQUIVALENT TO ALL BOUNDARIES

ANY DAMAGE TO EXISTING &/OR ADJOINING PROPERTY &/OR SERVICES IS TO BE MADE GOOD WITH MINIMAL IF ANY INCONVENIENCE TO ALL PROPRIETORS. IF ANY DAMAGE IS DUE TO NEGLIGENCE, IT IS TO BE RECTIFIED AT THE COST OF THE NEGLIGENT PARTY WHICH CAUSED THAT DAMAGE.

METHOD OF SUPPORT OF EXCAVATION ADJACENT TO ADJOINING PROPERTIES TO ENG'S DETAILS AND IT IS TO BE CERTIFIED BY A CERTIFIER ACCREDITED IN CIVIL ENGINEERING

VEHICLES CARRYING LOOSE BUILDING MATERIALS TO BE COVERED IN COMPLIANCE WITH ROAD TRAFFIC REGULATIONS. SAFE ACCESS FOR HEAVY EQUIPMENT PLANT AND MATERIALS DELIVERY.


DEMOLISH & REMOVE FROM THE SITE. AS PER THE SPECIFICATION, THE COUNCIL REQUIREMENTS & AS. 2601 ALL THE EXISTING BUILDINGS, CARPORT, FENCES, DRIVEWAY, PATHS AND THE LIKE, AS SHOWN HATCHED AND/OR AS REQUIRED TO ACHIEVE THE PROPOSED WORK. DISCONNECT, CAP OFF & SEAL ALL REDUNDANT SERVICES PRIOR TO THE COMMENCEMENT OF DEMOLITION

LEGEND

 TO BE DEMOLISHED TO COMPLY WITH AS 2601-2001

IMPORTANT CONSTRUCTION NOTES:

- REFER TO BCA REPORT FOR BUILDING REQUIREMENTS / PERFORMANCE SOLUTION / BUILDING UPGRADE.
- REFER TO FER REPORT PREAPRED BY FE CONSULTING P/L FOR PERFORMANCE SOLUTION / CONSTRUCTION UPGRADE.
- SITE AFFECTED BY BUSHFIRE PRONE. BAL 12.5 RATED MATERIALS MUST BE USED TO COMPLY WITH THE BUSHFIRE ASSESSMENT REPORT.

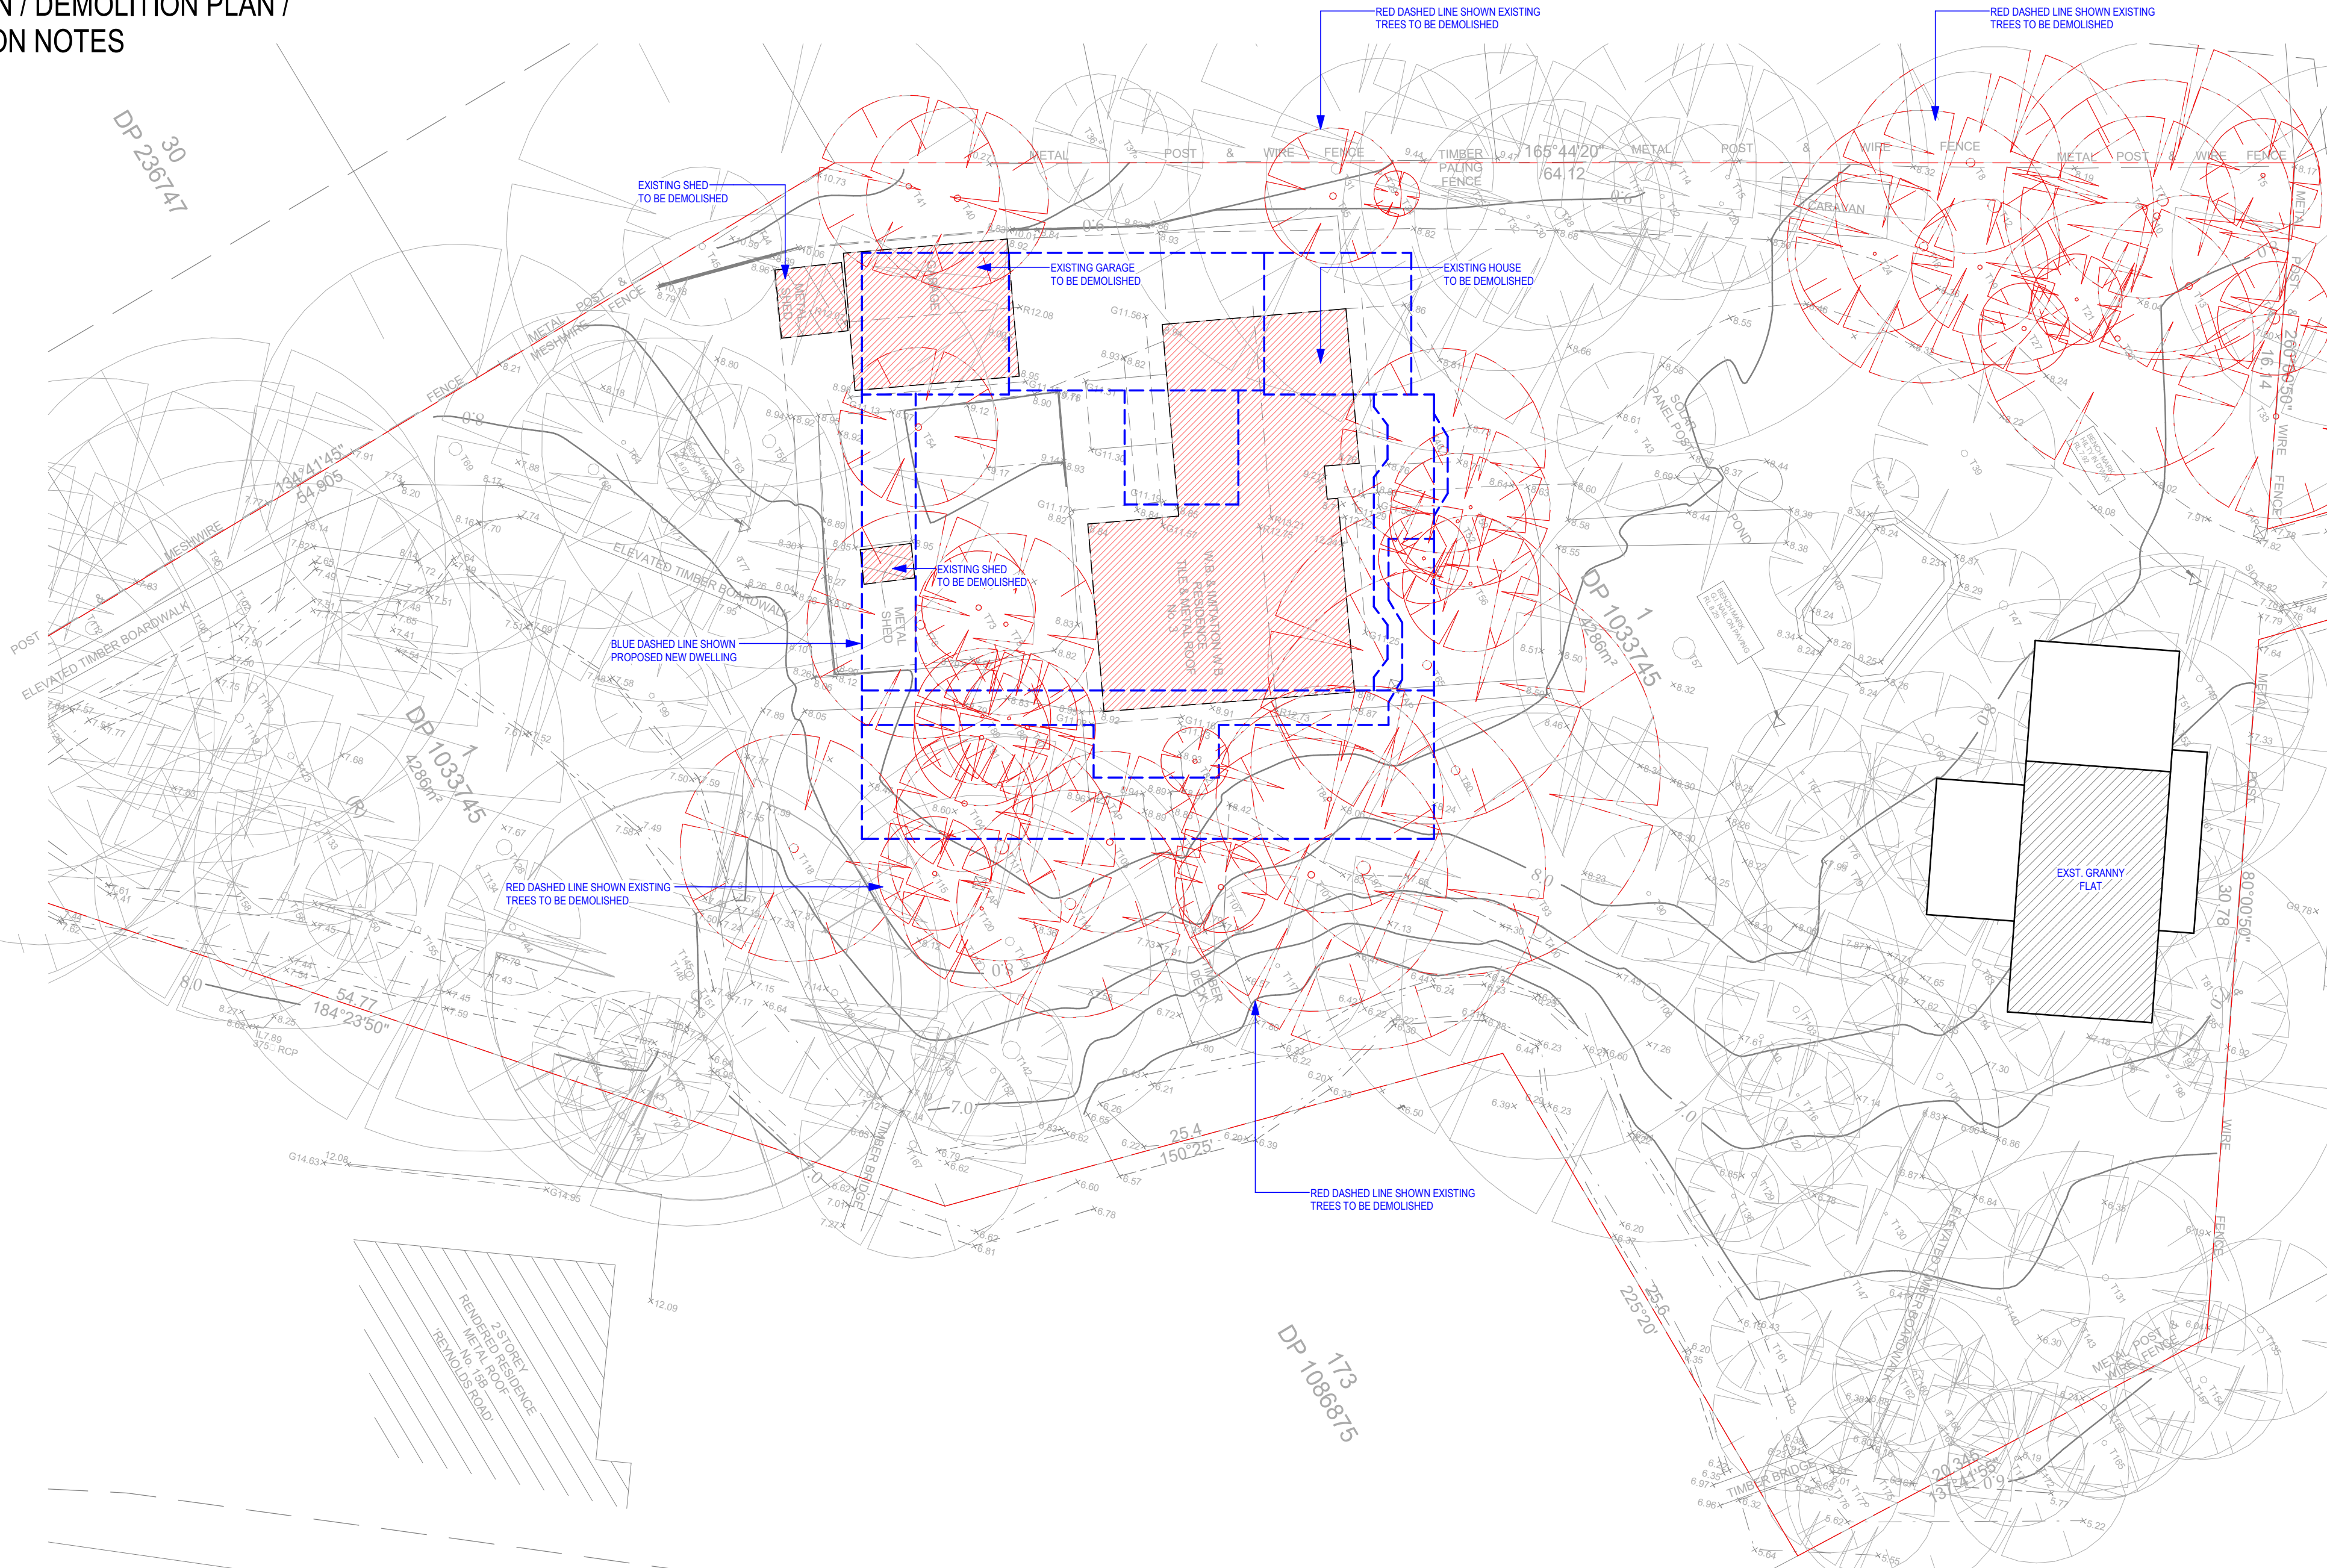

1 DEMOLITION PLAN
1 : 200

©THIS DRAWING IS THE PROPERTY OF LT DESIGN & CONSULTING PTY LTD AND WE RESERVE THE COPYRIGHT TO ALL OUR DESIGNS WHICH CANNOT BE REPRODUCED (IN PART OR IN WHOLE) BEFORE FIRST OBTAINING WRITTEN CONSENT. CONTRAVENTION WILL BE PROSECUTED

● FIGURED DIMENSIONS TO BE TAKEN IN PREFERENCE TO SCALE.

● BUILDERS' WORK TO COMPLY WITH THE LATEST BCA AND ITS AMENDMENTS AND RELEVANT AUSTRALIAN STANDARDS REFERRED WITHIN.

No.	Description	Date
1	REVISE AS PER COUNCIL REQUIREMENTS	22/03/2025



Building Design | 3D Modeling | Drafting | Detailing



BUILDING DESIGNERS AUSTRALIA

Accreditation No: 6302
Shop 6A/80 Thorneby Rd, Fairfield West
0414 891 998 - Le@LTDesign.net.au

DRAWING:
DEMOLITION PLAN

CLIENT & PROJECT: LOT 1 IN DP 1033745
CONSTRUCTION CERTIFICATE FOR DOUBLE STOREY DWELLING
AT NO.3 GILL AVENUE, AVOCA BEACH, NSW 2251

CONSTRUCTION CERTIFICATE

DATE:
22/03/2025
DWG NO:
CC-03

SCALE: 1 : 200 (A2)



DRW BY: LT

- LOH : LIFT OFF HINGES DOOR TO COMPLY WITH NCC 2022
- SA : SMOKE ALARM TO COMPLY WITH AS.3786
- FW : FLOOR WASTE
- MV : MECHANICAL VENTILATION SYSTEM
- L.WO : LINE OF WALL OVER
- B.O : BEAM OVER

IMPORTANT CONSTRUCTION NOTES:

- REFER TO BCA REPORT FOR BUILDING REQUIREMENTS / PERFORMANCE SOLUTION / BUILDING UPGRADE.
- REFER TO FER REPORT PREPARED BY FE CONSULTING P/L FOR PERFORMANCE SOLUTION / CONSTRUCTION UPGRADE.
- SITE AFFECTED BY BUSHFIRE PRONE. BAL 12.5 RATED MATERIALS MUST BE USED TO COMPLY WITH THE BUSHFIRE ASSESSMENT REPORT.

© THIS DRAWING IS THE PROPERTY OF LT DESIGN & CONSULTING PTY LTD AND WE RESERVE THE COPYRIGHT TO ALL OUR DESIGNS WHICH CANNOT BE REPRODUCED (IN PART OR IN WHOLE) BEFORE FIRST OBTAINING WRITTEN CONSENT. CONTRAVENTION WILL BE PROSECUTED

• FIGURED DIMENSIONS TO BE TAKEN IN PREFERENCE TO SCALE.

• BUILDERS' WORK TO COMPLY WITH THE LATEST BCA AND ITS AMENDMENTS AND RELEVANT AUSTRALIAN STANDARDS REFERRED WITHIN.

No.	Description	Date
1	REVISE AS PER COUNCIL REQUIREMENTS	22/03/2025



Building Design | 3D Modeling | Drafting | Detailing



Accreditation No: 6302
Shop 6A/80 Thorneys Rd, Fairfield West
0414 891 998 - Le@LTDesign.net.au

1 PROPOSED GROUND FLOOR PLAN
1 : 100

DRAWING: PROPOSED GROUND FLOOR PLAN


CLIENT & PROJECT: LOT 1 IN DP 1033745

CONSTRUCTION CERTIFICATE FOR DOUBLE STOREY DWELLING AT NO.3 GILL AVENUE, AVOCA BEACH, NSW 2251

CONSTRUCTION CERTIFICATE

DATE: 22/03/2025	DRW BY: LT
DWG NO: CC-04	SCALE: 1 : 100 (A2)



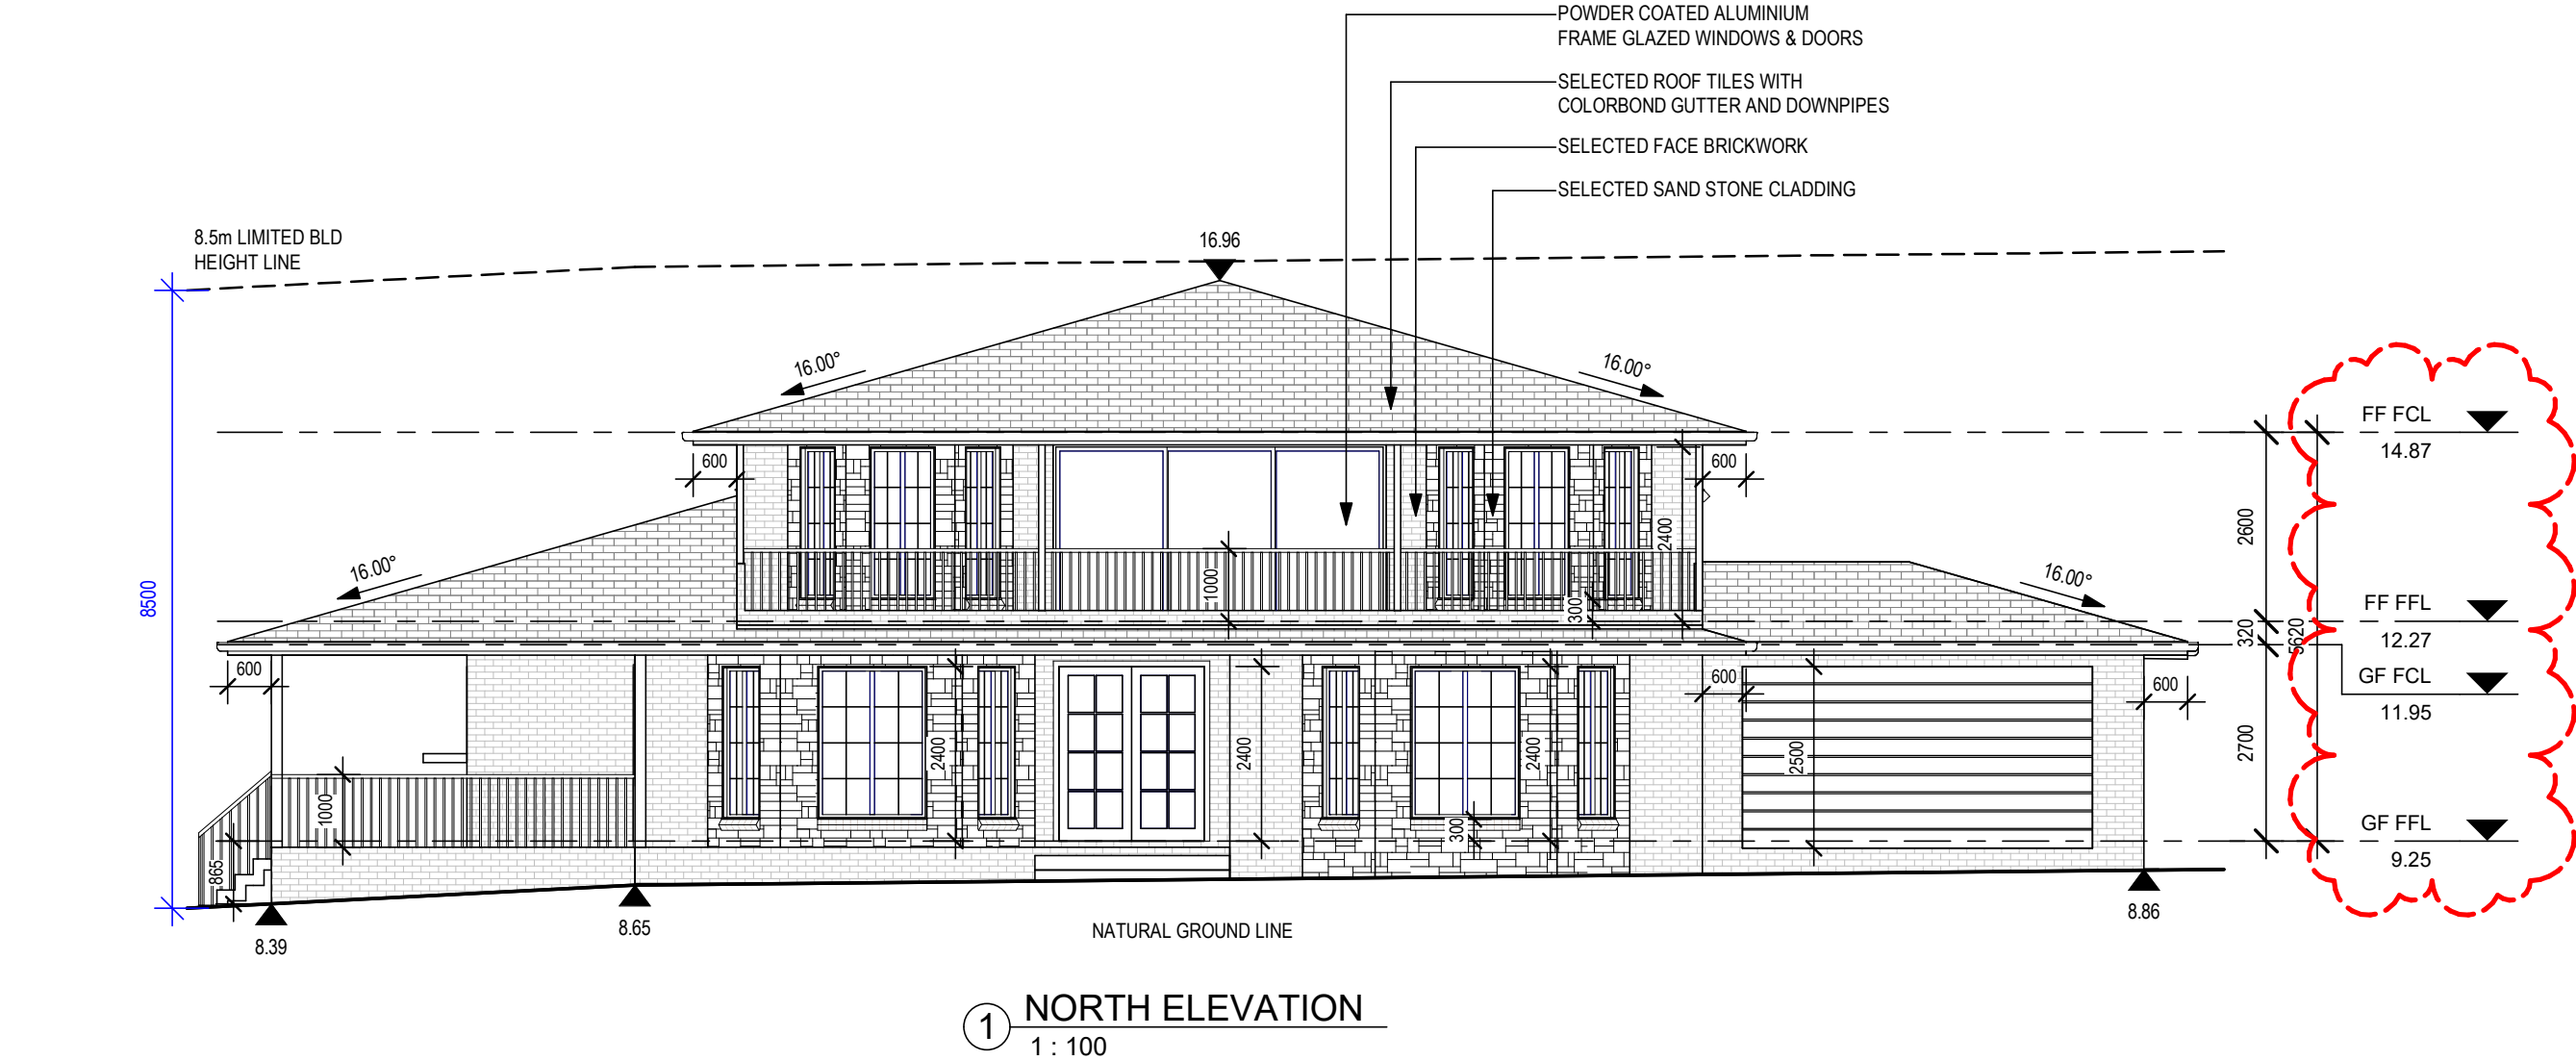

CONDENSATION MANAGEMENT:

(1)An exhaust system installed in a kitchen, bathroom, sanitary compartment or laundry must have a minimum flow rate of—

(a)25 L/s for a bathroom or sanitary compartment; and

(b)40 L/s for a kitchen or laundry.

(2)Exhaust from a kitchen, kitchen range hood, bathroom, sanitary compartment or laundry must discharge directly or via a shaft or duct to outdoor air.

(3)Where a venting clothes dryer is installed, it must discharge directly or via a shaft or duct to outdoor air.

(4)An exhaust system that is not run continuously and is serving a bathroom or sanitary compartment that is not ventilated in accordance with 10.6.2(a) must—

(a)be interlocked with the room's light switch; and

(b)include a run-on timer so that the exhaust system continues to operate for 10 minutes after the light switch is turned off.

(5)Except for rooms that are ventilated in accordance with 10.6.2(a), a room with an exhaust system in accordance with (1) must be provided with make-up air—

(a)via openings to an adjacent room with a free area of 14,000 mm²; or in accordance with AS 1668.2.


Window Schedule			
Mark	Width	Height	Orientation
W01	600	2100	NORTH
W02	1500	2100	NORTH
W03	600	2100	NORTH
W04	600	2100	NORTH
W05	1500	2100	NORTH
W06	600	2100	NORTH
W07	4000	1200	WEST
W08	1500	2100	WEST
W09	4000	1200	SOUTH
W10	2400	1200	SOUTH
W11	600	900	EAST
W12	600	2100	NORTH
W13	900	2100	NORTH
W14	600	2100	NORTH
W15	600	2100	NORTH
W16	900	2100	NORTH
W17	600	2100	NORTH
W18	2400	600	WEST
W19	600	600	WEST
W20	1500	600	WEST
W21	2400	600	WEST
W22	2400	600	SOUTH
W23	2400	600	SOUTH
W24	3000	600	EAST
W25	1800	2100	EAST
W26	3000	600	EAST

NOTE:
WEEPOLDS TO COMPLY WITH AS 3700, AS 4773 AND OTHER RELEVANT STANDARD

NOTE:
EAVES ENCRACHING WITHIN 900mm OF AN ALLOTMENT BOUNDARY AND 1800mm FROM ANOTHER BUILDING TO BE NON-COMBUSTILE

IMPORTANT CONSTRUCTION NOTES:

- REFER TO BCA REPORT FOR BUILDING REQUIREMENTS / PERFORMANCE SOLUTION / BUILDING UPGRADE.
- REFER TO FER REPORT PREAPRED BY FE CONSULTING P/L FOR PERFORMANCE SOLUTION / CONSTRUCTION UPGRADE.
- SITE AFFECTED BY BUSHFIRE PRONE. BAL 12.5 RATED MATERIALS MUST BE USED TO COMPLY WITH THE BUSHFIRE ASSESSMENT REPORT.

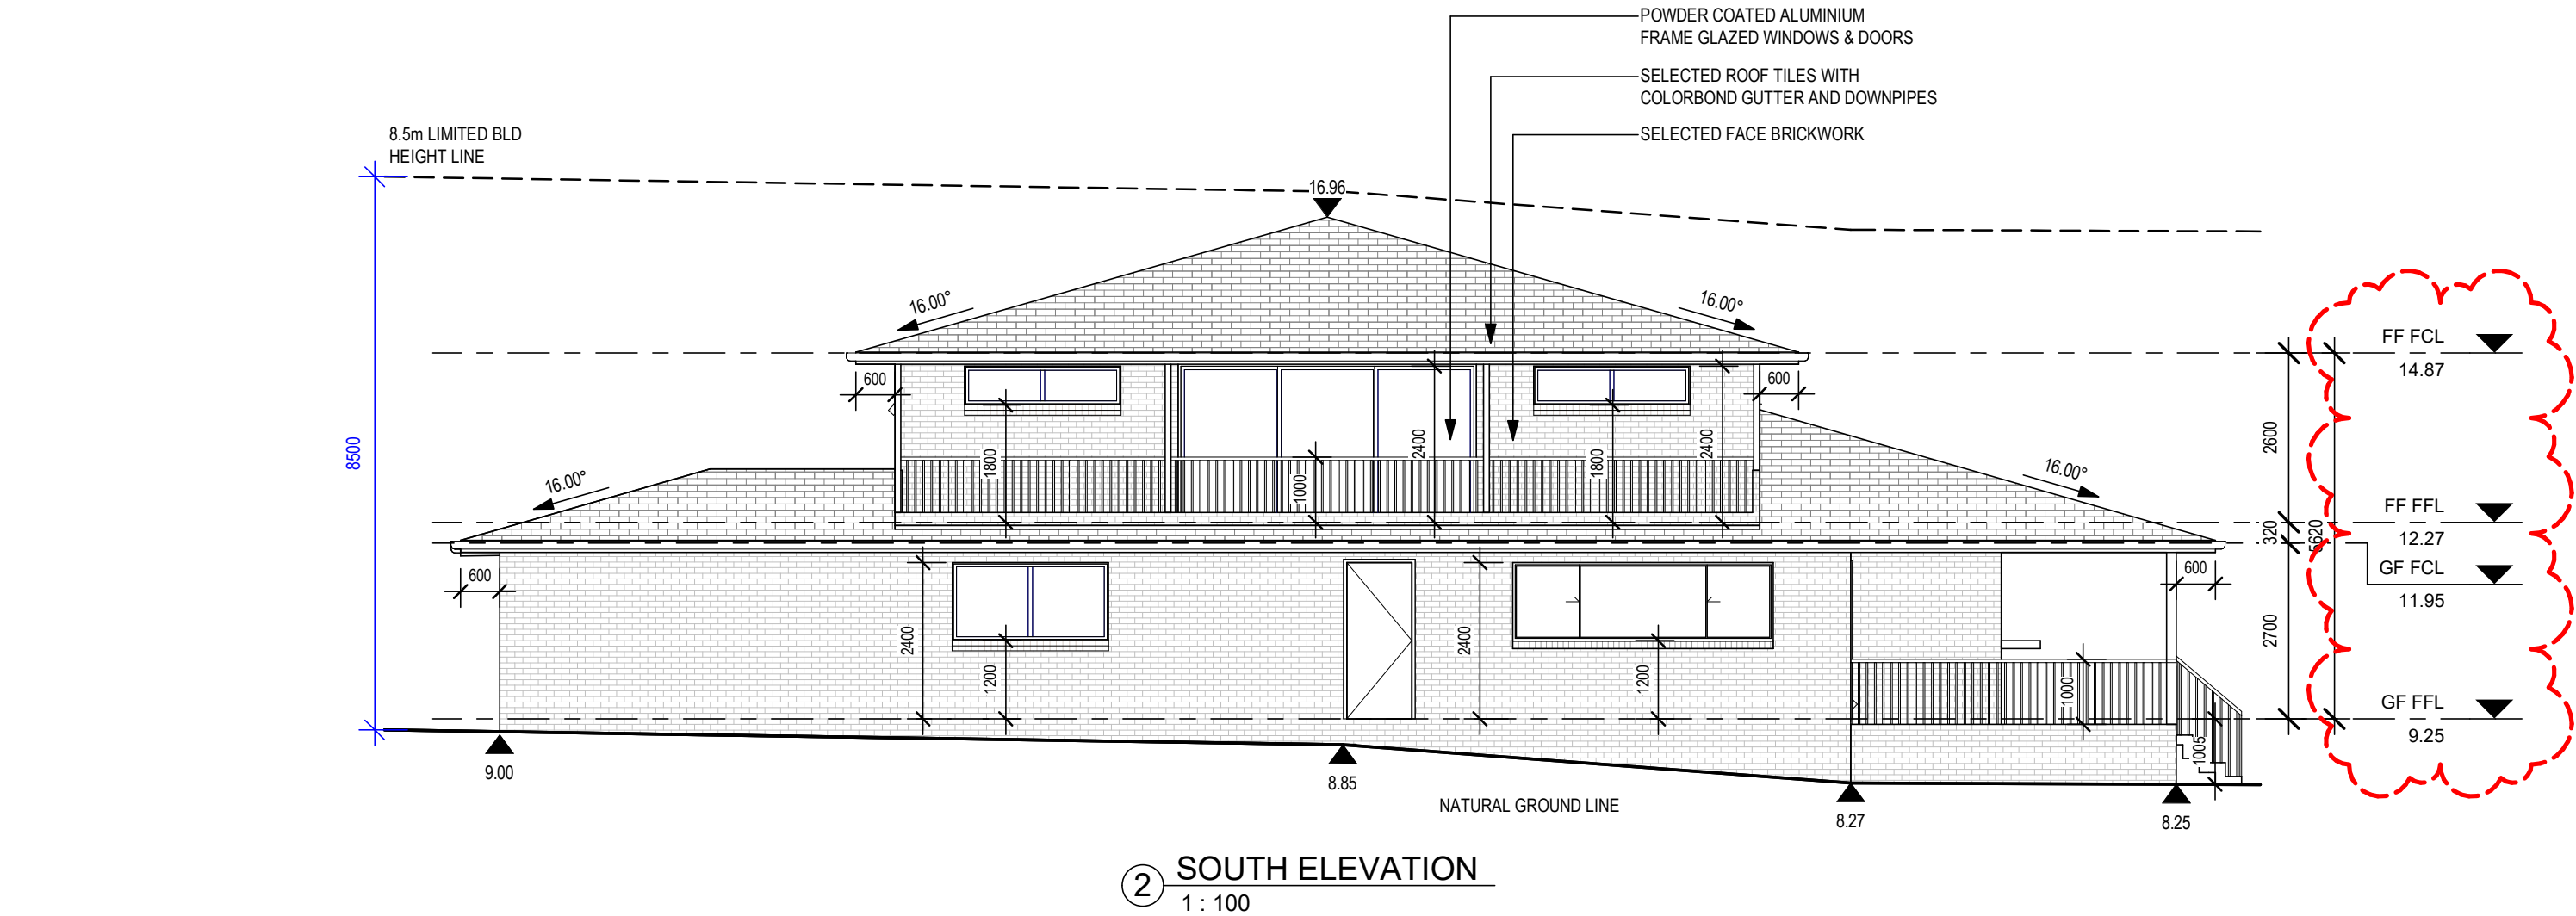

© THIS DRAWING IS THE PROPERTY OF LT DESIGN & CONSULTING PTY LTD AND WE RESERVE THE COPYRIGHT TO ALL OUR DESIGNS WHICH CANNOT BE REPRODUCED (IN PART OR IN WHOLE) BEFORE FIRST OBTAINING WRITTEN CONSENT. CONTRAVENTION WILL BE PROSECUTED

- FIGURED DIMENSIONS TO BE TAKEN IN PREFERENCE TO SCALE.
- BUILDERS' WORK TO COMPLY WITH THE LATEST BCA AND ITS AMENDMENTS AND RELEVANT AUSTRALIAN STANDARDS REFERRED WITHIN.

No.	Description	Date
1	REVISE AS PER COUNCIL REQUIREMENTS	22/03/2025



LT
DESIGN



bda
BUILDING
DESIGNERS
AUSTRALIA

Accreditation No: 6302
Shop 6A/80 Thorne Rd, Fairfield West
0414 891 998 - Le@LTDesign.net.au

DRAWING:
NORTH & SOUTH ELEVATIONS

CLIENT & PROJECT: LOT 1 IN DP 1033745

CONSTRUCTION CERTIFICATE FOR DOUBLE STOREY DWELLING AT NO.3 GILL AVENUE, AVOCA BEACH, NSW 2251


CONSTRUCTION CERTIFICATE

DATE:
22/03/2025

DWG NO:
CC-06

SCALE:
1 : 100 (A2)

DRW BY:
LT

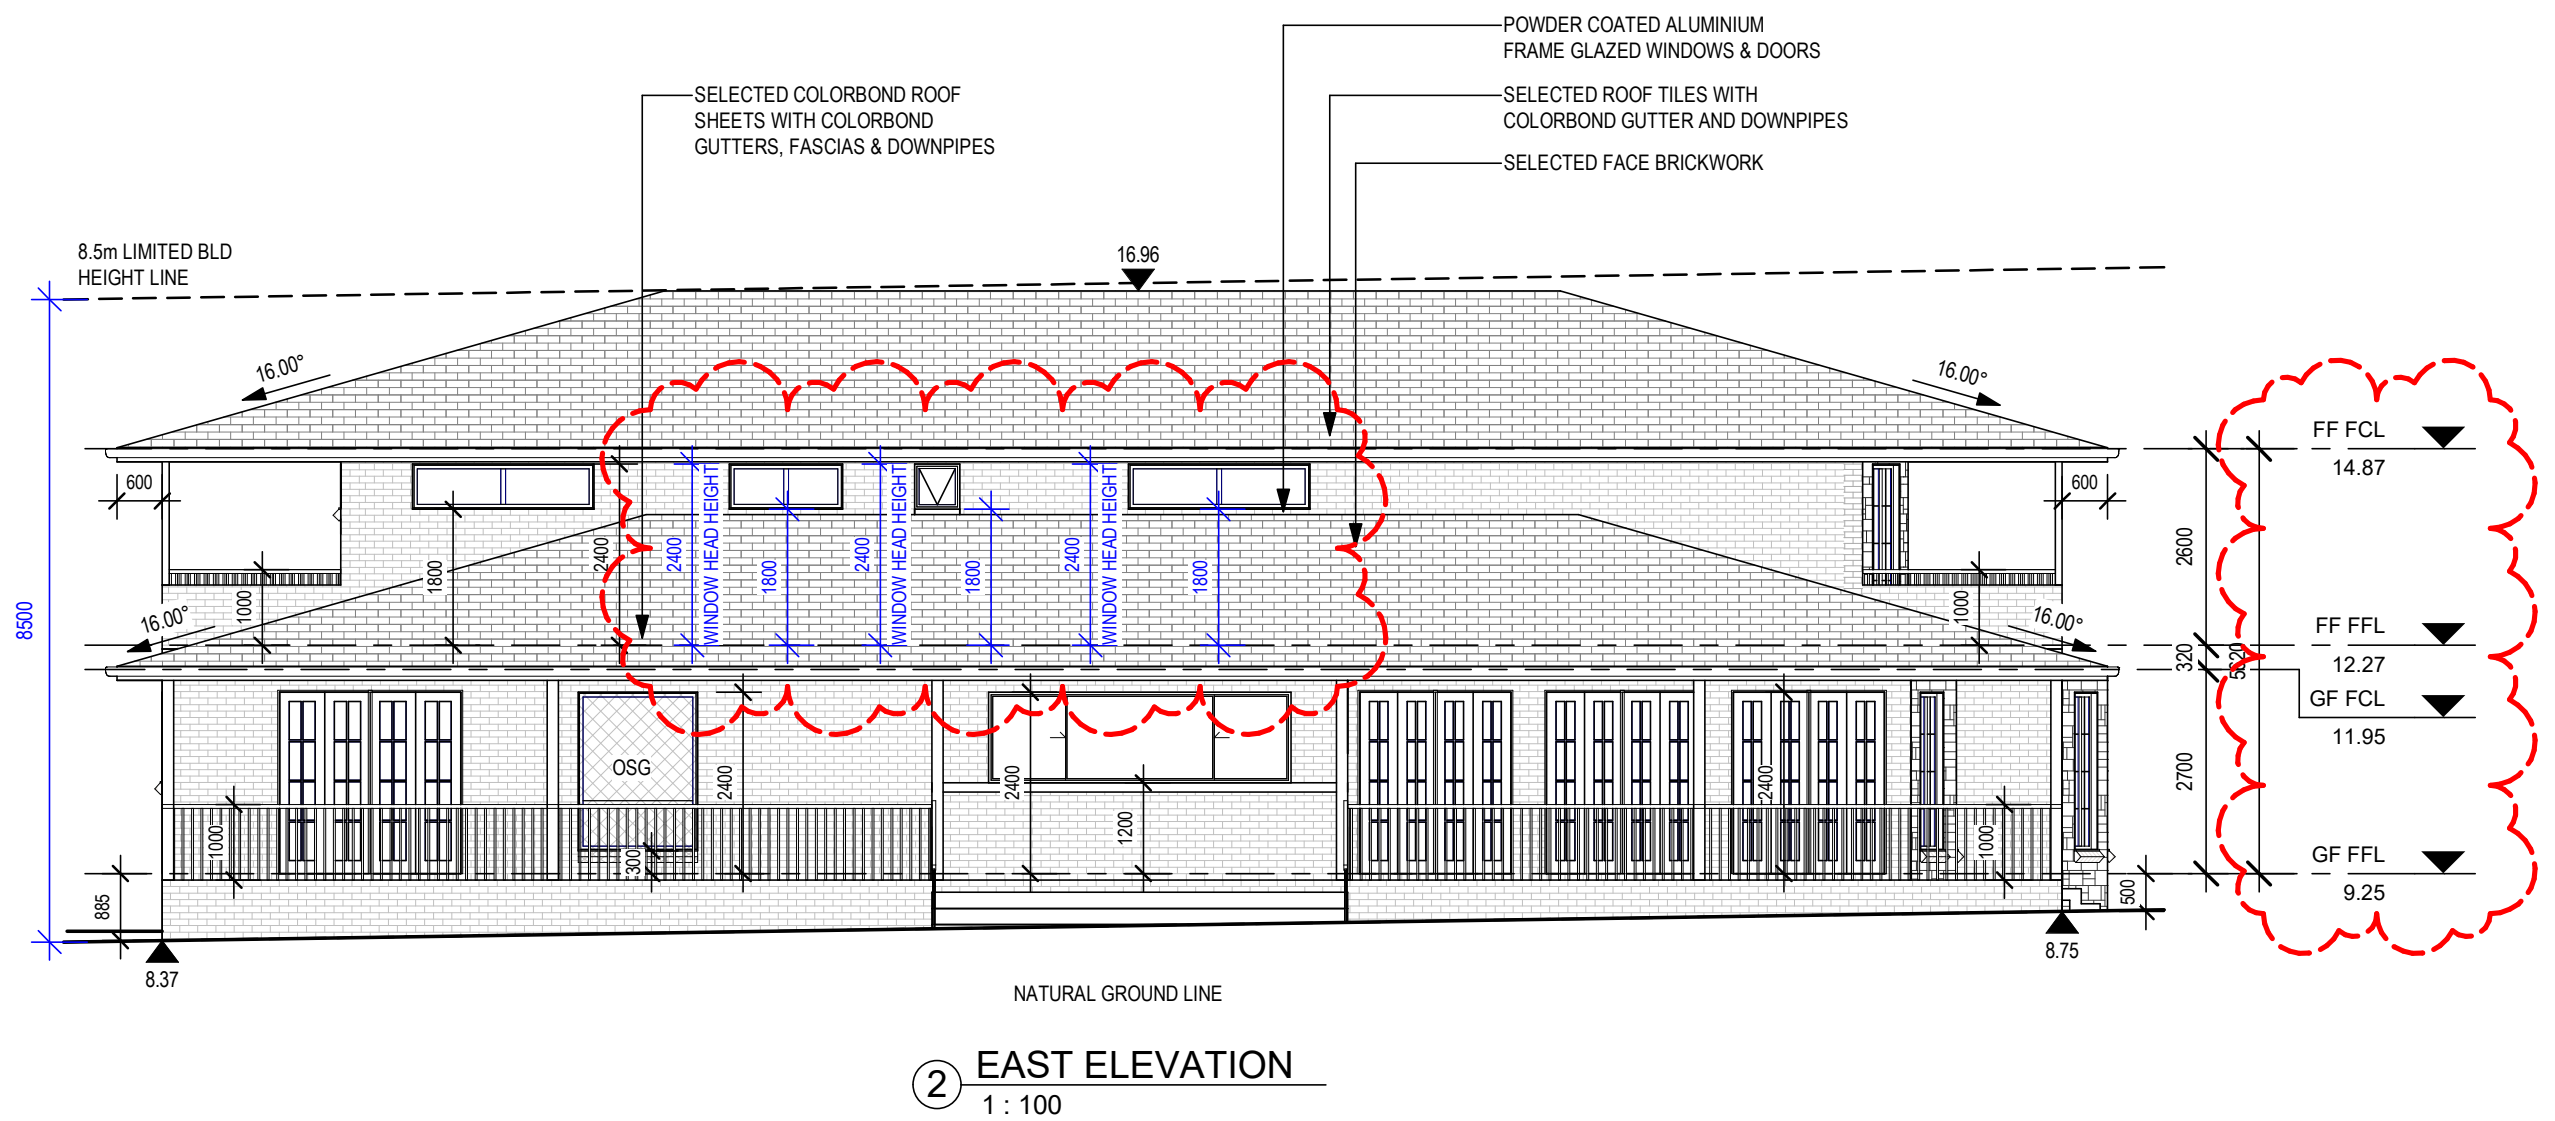

NOTE:
EAVES ENCROACHING WITHIN 900mm
OF AN ALLOTMENT BOUNDARY AND
1800mm FROM ANOTHER BUILDING
TO BE NON-COMBUSTILE

© THIS DRAWING IS THE PROPERTY OF LT DESIGN & CONSULTING PTY LTD AND WE RESERVE THE COPYRIGHT TO ALL OUR DESIGNS WHICH CANNOT BE REPRODUCED (IN PART OR IN WHOLE) BEFORE FIRST OBTAINING WRITTEN CONSENT. CONTRAVENTION WILL BE PROSECUTED


- FIGURED DIMENSIONS TO BE TAKEN IN PREFERENCE TO SCALE.
- BUILDERS' WORK TO COMPLY WITH THE LATEST BCA AND ITS AMENDMENTS AND RELEVANT AUSTRALIAN STANDARDS REFERRED WITHIN.

No.	Description	Date
1	REVISE AS PER COUNCIL REQUIREMENTS	22/03/2025



 BUILDING DESIGNERS AUSTRALIA
 Accreditation No: 6302
 Shop 6A/80 Thorney Rd, Fairfield West
 0414 891 998 - Le@LTDesign.net.au
 Building Design | 3D Modeling | Drafting | Detailing

DRAWING: EAST & WEST ELEVATIONS		
CLIENT & PROJECT: LOT 1 IN DP 1033745 CONSTRUCTION CERTIFICATE FOR DOUBLE STOREY DWELLING AT NO.3 GILL AVENUE, AVOCA BEACH, NSW 2251	DATE: 22/03/2025 DWG NO: CC-07	
CONSTRUCTION CERTIFICATE		DRW BY: LT SCALE: 1 : 100 (A2)

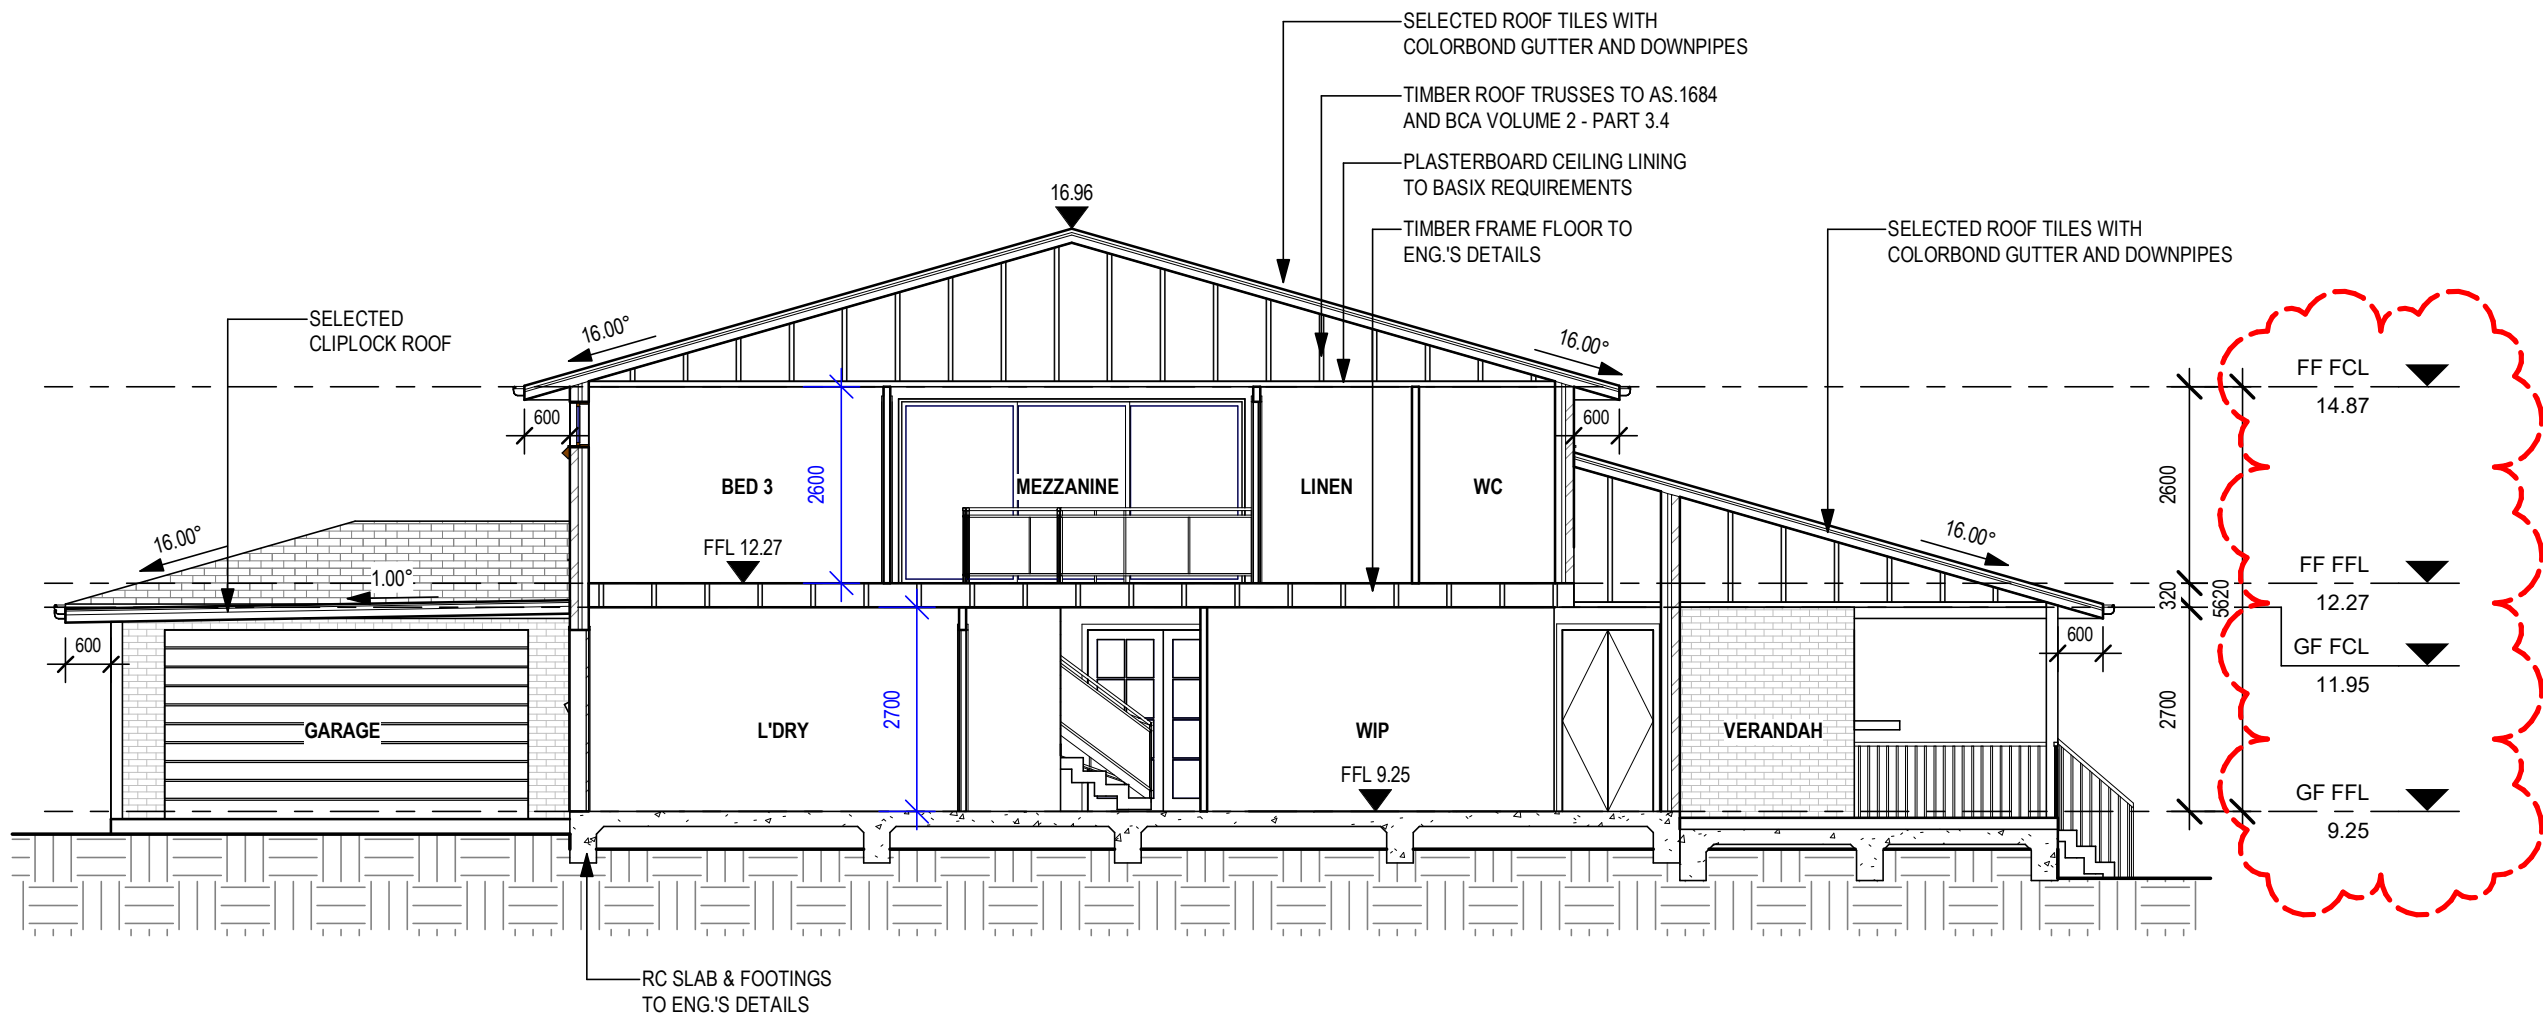

1 SECTION A-A
1 : 100

2	Clarify that timber boardwalk/pathway does not form part of this development consent The existing platforms/pathways circulating out from the existing dwelling and crossing the watercourse does not form part of this development consent. Condition reason: To clarify this aspect of the development is not related to this development
15	Protection of watercourse and ecological communities on land Identify the existing watercourse on all plans as an exclusion zone. Trees and native vegetation proposed for retention and those approved for removal must be clearly marked on all final engineering and landscaping plans. All fenced tree and watercourse protection areas must be clearly marked as "No Go Area" on all plans. The location of any threatened species and ecological communities must also be marked on all plans. Condition reason: Protection of the environment
30	Pool fence Erect or install prior to the swimming pool being filled with water all the required swimming pool safety barriers and gates in accordance with the approved plans and specifications and the provisions of the <i>Swimming Pools Act 1992</i> , Swimming Pools Regulation 2018 and Australian Standard AS 1926.1-2012, including sign displaying all warning notices required by Clause 10 (1) of the Swimming Pools Regulation 2018 must be permanently fixed and located in a prominent position in the immediate vicinity of the pool. Condition reason: To ensure swimming pool safety and protect the environment and amenity of the local area.

25	Dispose pool backwash and overflow Dispose filter backwash and overflow to the sewer. The sewer connection must be completed prior to the filling of the pool with water and in a manner that will not cause a nuisance, or where sewer is not available, the disposal of filter backwash must be discharged into a rubble absorption trench to the satisfaction of the Principal Certifier. Condition reason: To ensure swimming pool safety and protect the environment and amenity of the local area.
27	Floor level of construction Submit a report prepared by a registered Surveyor to the Principal Certifier at the ground floor level of construction of the building (prior to the pouring of concrete) indicating that the finished floor level is at RL 9.25 AHD, in accordance with the approved plans. An RL of 9.25AHD is the Maximum Probable Flood (PMF) event that is current under a recent flood study. Condition reason: To ensure buildings are positioned in the approved location and at the correct height.
28	No fill footprint building No fill other than that as indicated within the approved plans is permitted to be placed upon the site. Condition reason: Compliance with requirements is necessary during any construction works.

32	Environmental Protection works during construction Install a temporary fence to delineate the construction site from the water course, vegetation and habitat to be retained. In this instance, flagging bunting / reflector line will be sufficient. All fenced conservation areas are to be clearly marked as a "No Go Area" on the fencing itself. No clearing of vegetation, storage of vehicles or machinery, stockpiling, materials storage or unauthorised access is to occur within the fenced conservation area. Maintain the temporary fence around the conservation area. The fence must be maintained for the duration of construction works. EV013 Undertake clearing in accordance with the approved tree removal/retention survey plan provided in the supporting Arborist Report (<i>Advanced Arborist Reporting, July 2024</i>). Trees must be removed in such a manner so as to prevent damage to surrounding trees to be retained.EV015EV014 Utilise timber from felled native trees by: • Re-instating logs as ground habitat in areas of retained vegetation, and/or • Wood chip or tub grind into mulch for landscaping, soil stabilisation or bush regeneration, and/or • Using for firewood (but not piled burned on-site); and/or • Recycling for use in construction materials, furniture or fencing. EV022 Manage native fauna appropriately during clearing and construction phase of the approved works. Where, in spite of precautions, wildlife is injured, necessary action to treat the animal, which may include veterinary treatment or transfer of the animal to a volunteer wildlife carer group such as WIRES or Wildlife Arc is required. Condition reason: Protection of the environment.
----	---

37	Prevent flammable roof gutter Install a material or device to prevent the build-up of flammable material (such as leaf matter) within the roof gutters. The material or device must have a flammability index of not greater than 5 when tested in accordance with Australian Standard AS 1530.2-1993: Methods for fire tests on building materials, components and structures - Test for flammability of materials. The works are to be completed prior to issue of any Occupation Certificate. Condition reason: To protect the amenity of the local area.
38	Roof water drained Drain all roof water by a piped drainage line as illustrated within the stormwater management plans referenced within the condition of this development consent. Condition reason: To ensure appropriate provision for management and disposal of stormwater.

40	Insulate sound producing equipment Insulate and / or isolate the motor, filter, pump and all sound producing equipment or fitting associated with or forming part of the pool filtering system so as not to create an offensive noise to the occupants of the adjoining premises as defined in the <i>Protection of the Environment Operations Act 1997</i> . Condition reason: To protect the amenity of the local area.
41	Use of light to protect the environment Use external lighting that minimises overspill into retained vegetated areas. Condition reason: Protection of the environment.

NOTE:
EAVES ENCRoACHING WITHIN 900mm OF AN ALLoTMENT BOUNDARY AND 1800mm FROM ANoThER BUILDING To BE NON-COMBUSTILE

IMPORTANT CONSTRUCTION NOTES:
- REFER TO BCA REPORT FOR BUILDING REQUIREMENTS / PERFORMANCE SOLUTION / BUILDING UPGRADE.
- REFER TO FER REPORT PREAPRED BY FE CONSULTING P/L FOR PERFORMANCE SOLUTION / CONSTRUCTION UPGRADE.
- SITE AFFECTED BY BUSHFIRE PRONE. BAL 12.5 RATED MATERIALS MUST BE USED TO COMPLY WITH THE BUSHFIRE ASSESSMENT REPORT.

©THIS DRAWING IS THE PROPERTY OF LT DESIGN & CONSULTING PTY LTD AND WE RESERVE THE COPYRIGHT TO ALL OUR DESIGNS WHICH CANNOT BE REPRODUCED (IN PART OR IN WHOLE) BEFORE FIRST OBTAINING WRITTEN CONSENT. CONTRAVENTION WILL BE PROSECUTED

• FIGURED DIMENSIONS TO BE TAKEN IN PREFERENCE TO SCALE.

• BUILDERS' WORK TO COMPLY WITH THE LATEST BCA AND ITS AMENDMENTS AND RELEVANT AUSTRALIAN STANDARDS REFERRED WITHIN.

No.	Description	Date
1	REVISE AS PER COUNCIL REQUIREMENTS	22/03/2025



Building Design | 3D Modeling | Drafting | Detailing



BUILDING DESIGNERS AUSTRALIA
Accreditation No: 6302
Shop 6A/80 Thorney Rd, Fairfield West
0414 891 998 - Le@LTDesign.net.au

DRAWING:

SECTION

CLIENT & PROJECT: LOT 1 IN DP 1033745

CONSTRUCTION CERTIFICATE FOR DOUBLE STOREY DWELLING
AT NO.3 GILL AVENUE, AVOCA BEACH, NSW 2251

CONSTRUCTION CERTIFICATE

DATE:
22/03/2025
DWG NO:
CC-08

DRW BY:
LT

SCALE: 1 : 100 (A2)



SWIMMING POOL FENCE NOTES:

A) THE SWIMMING POOL SAFETY FENCING MUST STRICTLY ADHERE TO THE DESIGN AND LOCATION APPROVED WITH THE DEVELOPMENT CONSENT, AND ANY CONDITIONS OF THE DEVELOPMENT CONSENT;

B) FENCES AND GATES MUST STRICTLY COMPLY WITH AS1926-2012 – SWIMMING POOL SAFETY – PART 1: SAFETY BARRIERS FOR SWIMMING POOLS;

C) FENCING SHALL HAVE A MINIMUM EFFECTIVE HEIGHT OF 1.2M;

D) ALL SWIMMING POOL GATES SHALL BE SELF-CLOSING AND SELF-LATCHING. ALL GATES MUST OPEN OUTWARDS FROM THE SWIMMING POOL ENCLOSURE;

E) THE FILTRATION EQUIPMENT INCLUDING ANY COVER, HOUSING OR PIPE WORK, MUST NOT BE LOCATED WITHIN A DISTANCE OF 900MM FROM THE OUTSIDE FACE OF THE SWIMMING POOL SAFETY FENCING ENCLOSURE, NOR WITHIN 300MM FROM THE INSIDE OF THE SWIMMING POOL SAFETY FENCING ENCLOSURE (WHERE FOOTHOLDS ARE POSSIBLE); AND

F) BOUNDARY FENCING FORMING PART OF THE SWIMMING POOL SAFETY FENCING SHALL MAINTAIN A MINIMUM EFFECTIVE HEIGHT OF 1.8M AND A 0.9M NON CLIMBABLE ZONE (MEASURED FROM THE TOP OF THE INSIDE OF THE BARRIER).


THE SWIMMING POOL OR SPA MUST BE FENCED SO THAT THE POOL IS EFFECTIVELY ISOLATED FROM THE DWELLING AND ADJOINING LANDS. THE SWIMMING POOL FENCE MUST COMPLY WITH THE FOLLOWING REQUIREMENTS:

IMPORTANT CONSTRUCTION NOTES:


- REFER TO BCA REPORT FOR BUILDING REQUIREMENTS / PERFORMANCE SOLUTION / BUILDING UPGRADE.
- REFER TO FER REPORT PREAPRED BY FE CONSULTING P/L FOR PERFORMANCE SOLUTION / CONSTRUCTION UPGRADE.
- SITE AFFECTED BY BUSHFIRE PRONE. BAL 12.5 RATED MATERIALS MUST BE USED TO COMPLY WITH THE BUSHFIRE ASSESSMENT REPORT.

NOTE:


- NO ITEMS OR STRUCTURES TO BE CONSTRUCTED OR INSTALLED WITHIN 900mm OF POOL FENCE TO COMPLY WITH AS 1926.1-2012

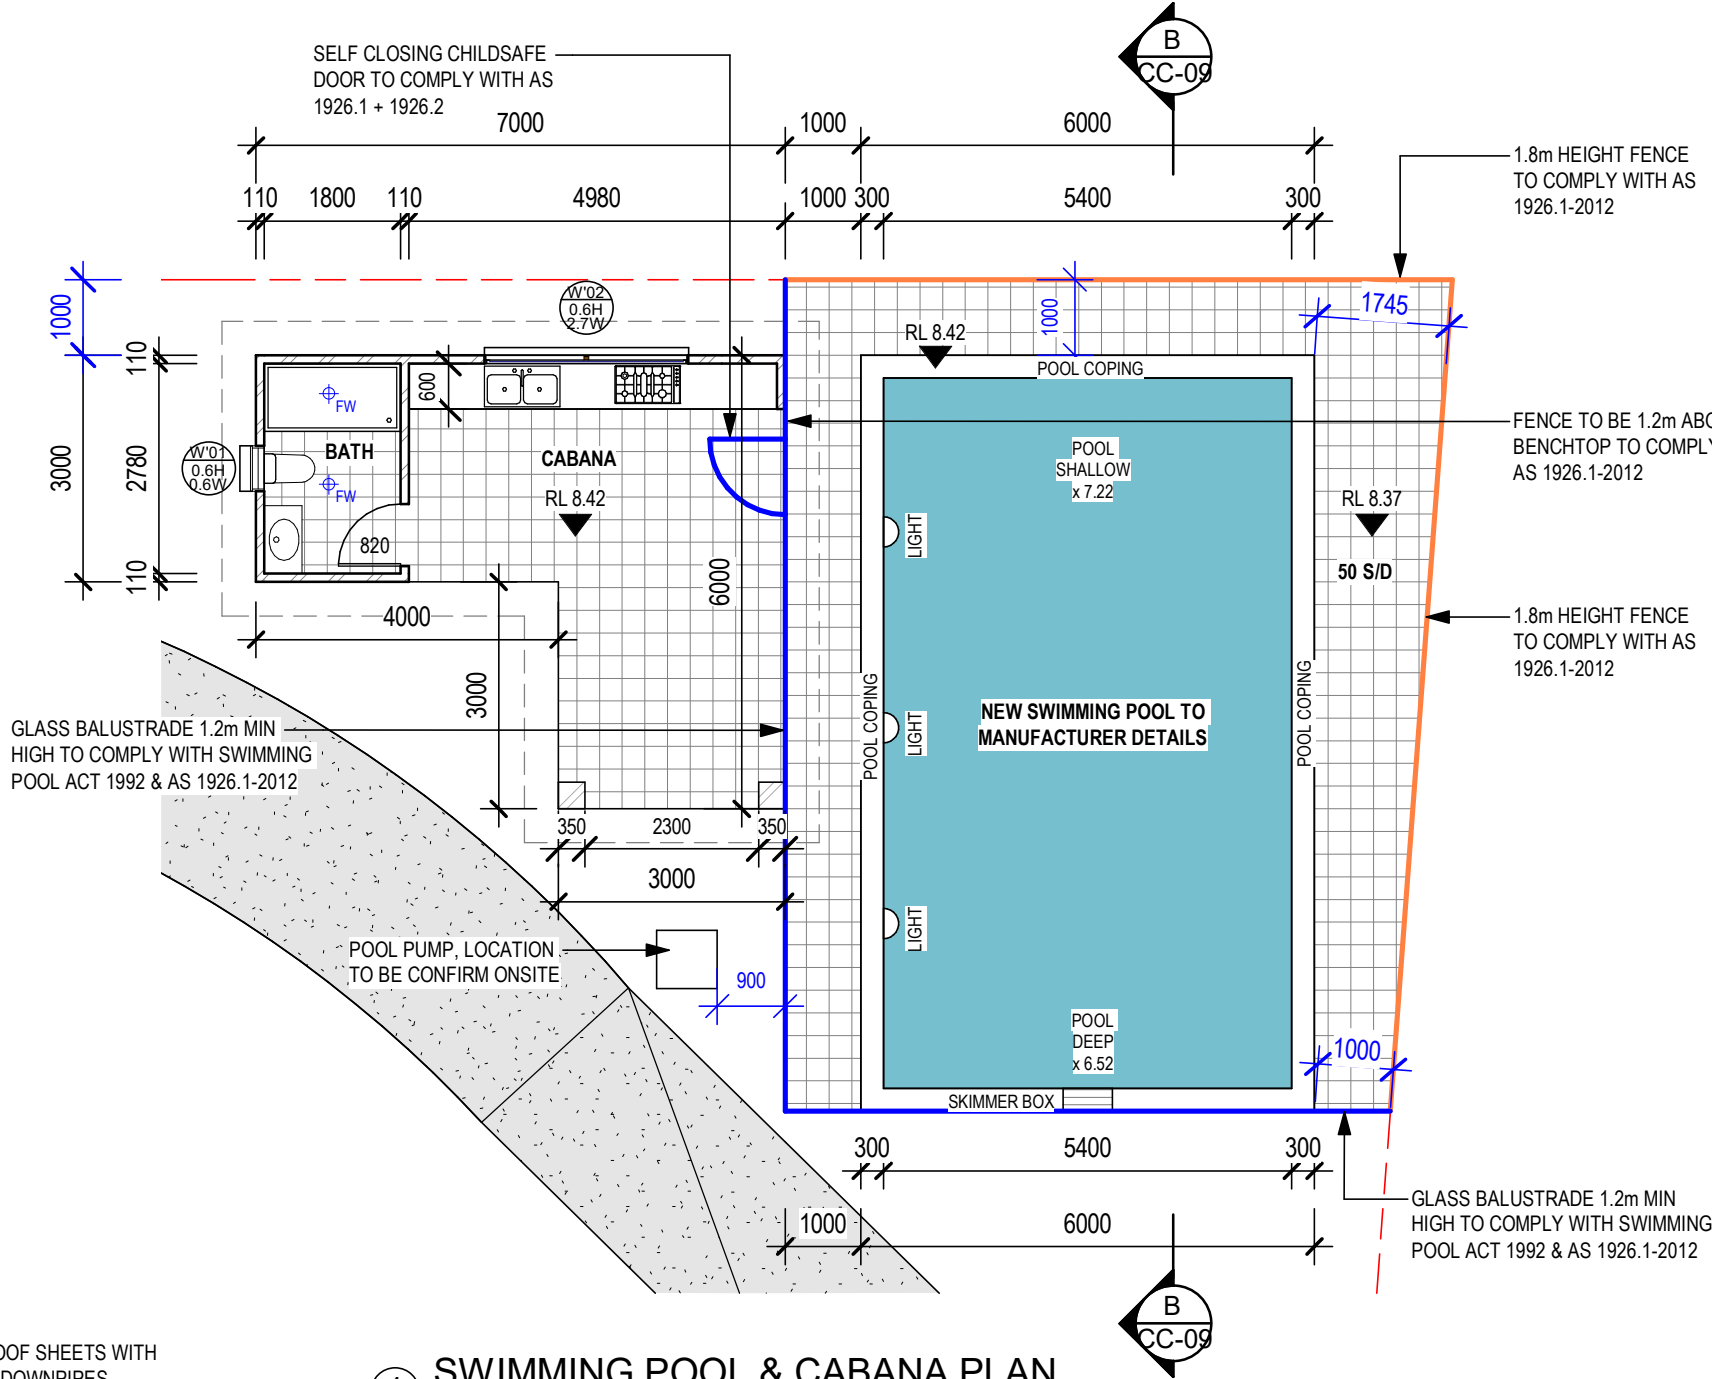


1 SWIMMING POOL & CABANA PLAN
1 : 100

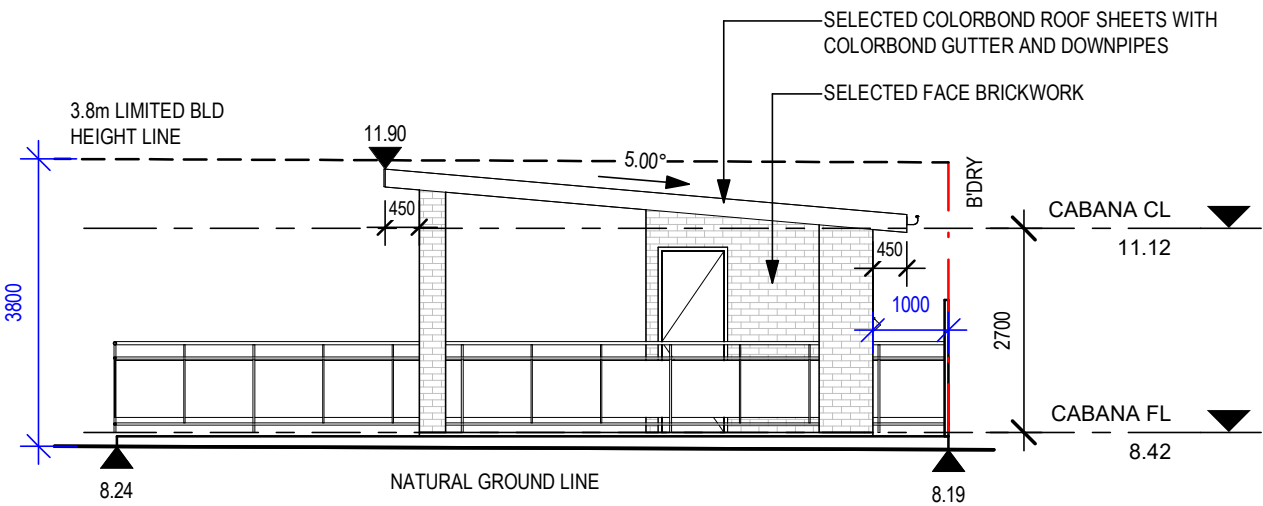


2 CABANA NORTH ELEVATION
1 : 100

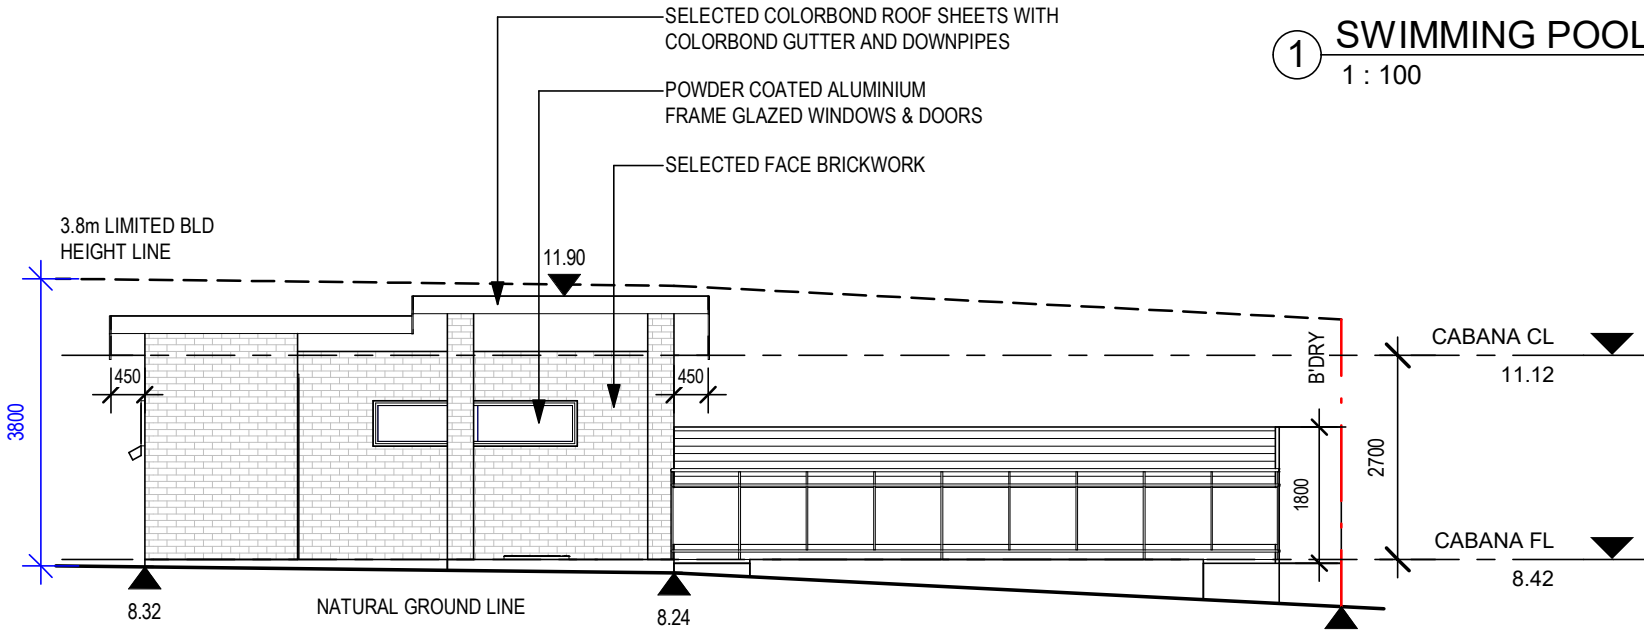


3 CABANA EAST ELEVATION
1 : 100

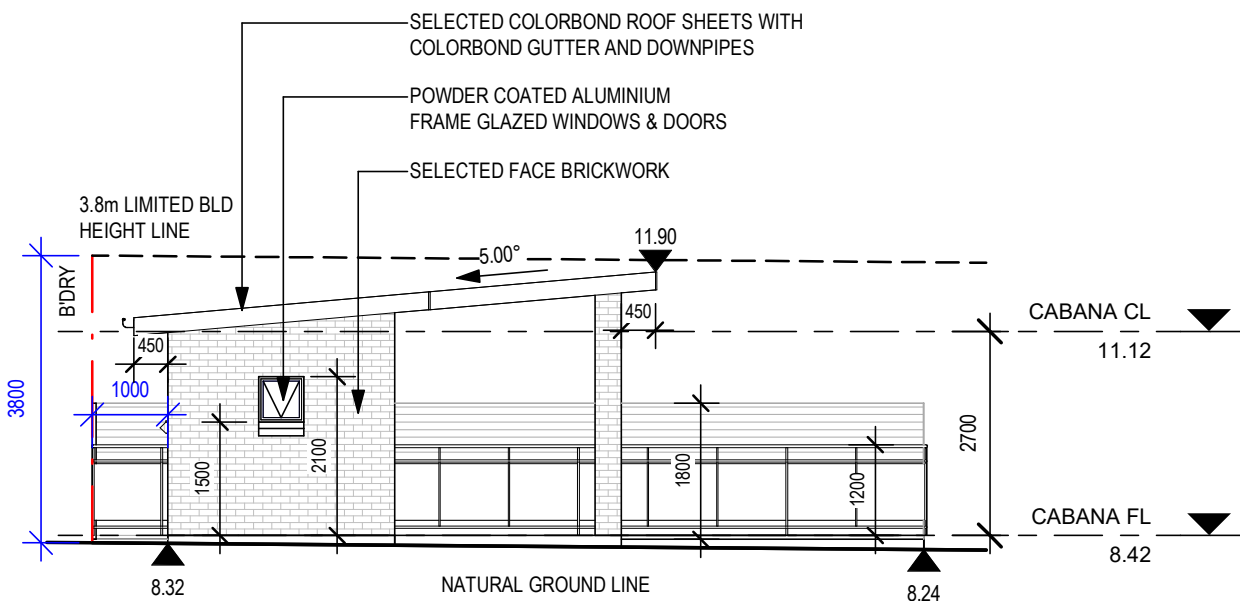

4 CABANA SOUTH ELEVATION
1 : 100

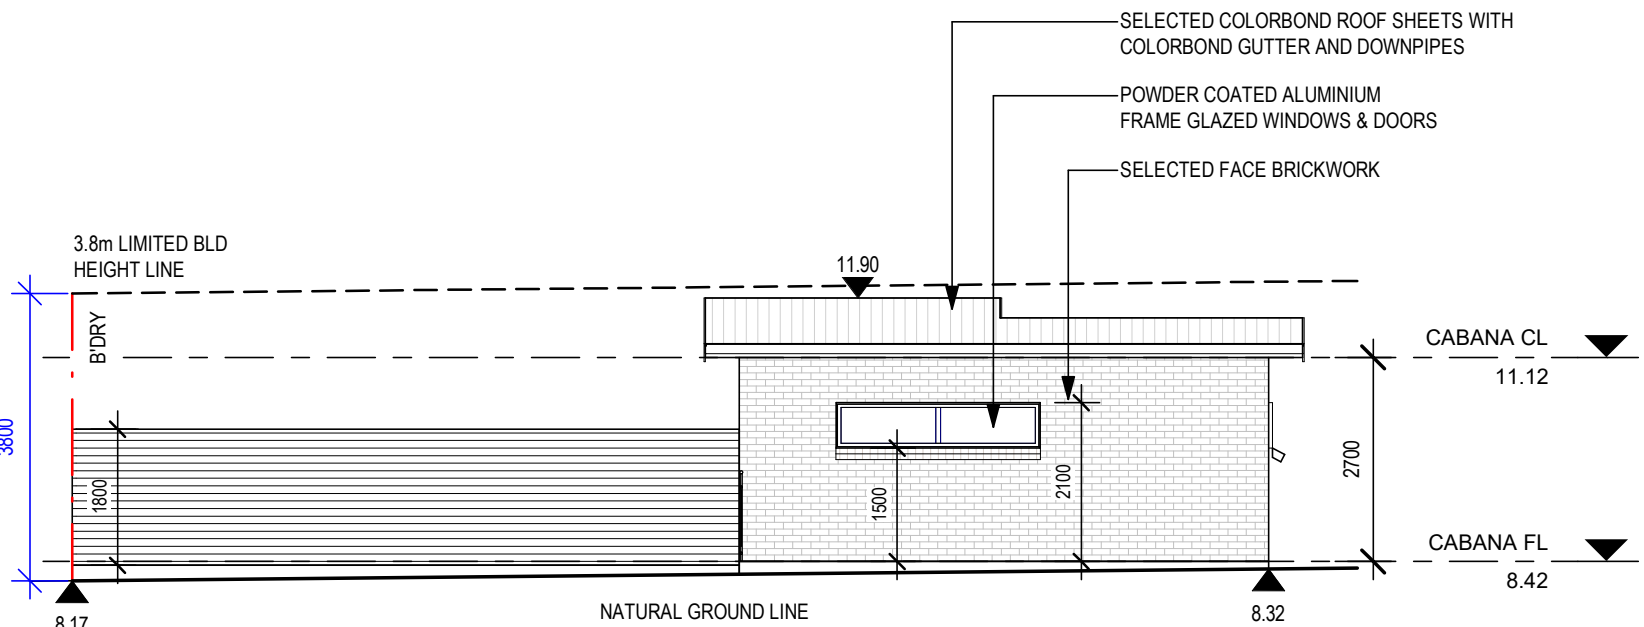

5 CABANA WEST ELEVATION
1 : 100

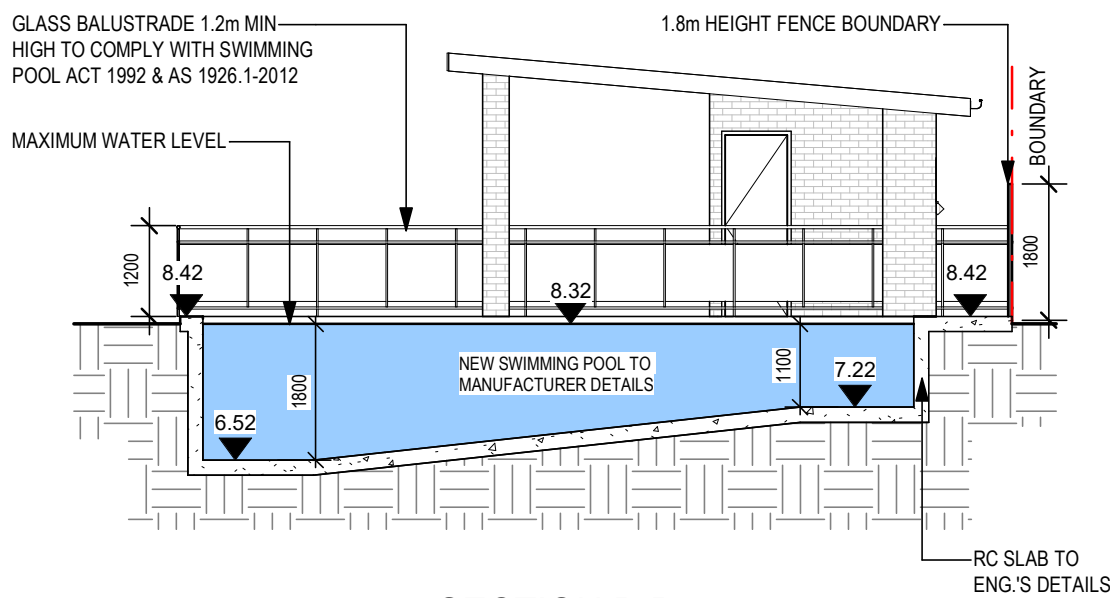

6 SECTION B-B
1 : 100

© THIS DRAWING IS THE PROPERTY OF LT DESIGN & CONSULTING PTY LTD AND WE RESERVE THE COPYRIGHT TO ALL OUR DESIGNS WHICH CANNOT BE REPRODUCED (IN PART OR IN WHOLE) BEFORE FIRST OBTAINING WRITTEN CONSENT. CONTRAVENTION WILL BE PROSECUTED

• FIGURED DIMENSIONS TO BE TAKEN IN PREFERENCE TO SCALE.

• BUILDERS' WORK TO COMPLY WITH THE LATEST BCA AND ITS AMENDMENTS AND RELEVANT AUSTRALIAN STANDARDS REFERRED WITHIN.

No.	Description	Date
1	REVISE AS PER COUNCIL REQUIREMENTS	22/03/2025



Building Design | 3D Modeling | Drafting | Detailing



Accreditation No: 6302
Shop 6A/80 Thorneys Rd, Fairfield West
0414 891 998 - Le@LTDesign.net.au

DRAWING:
SWIMMING POOL & CABANA DETAILS

CLIENT & PROJECT: LOT 1 IN DP 1033745
CONSTRUCTION CERTIFICATE FOR DOUBLE STOREY DWELLING
AT NO.3 GILL AVENUE, AVOCA BEACH, NSW 2251


CONSTRUCTION CERTIFICATE

DATE:
22/03/2025
DWG NO:
CC-09



DRW BY:
LT

SCALE: 1 : 100 (A2)

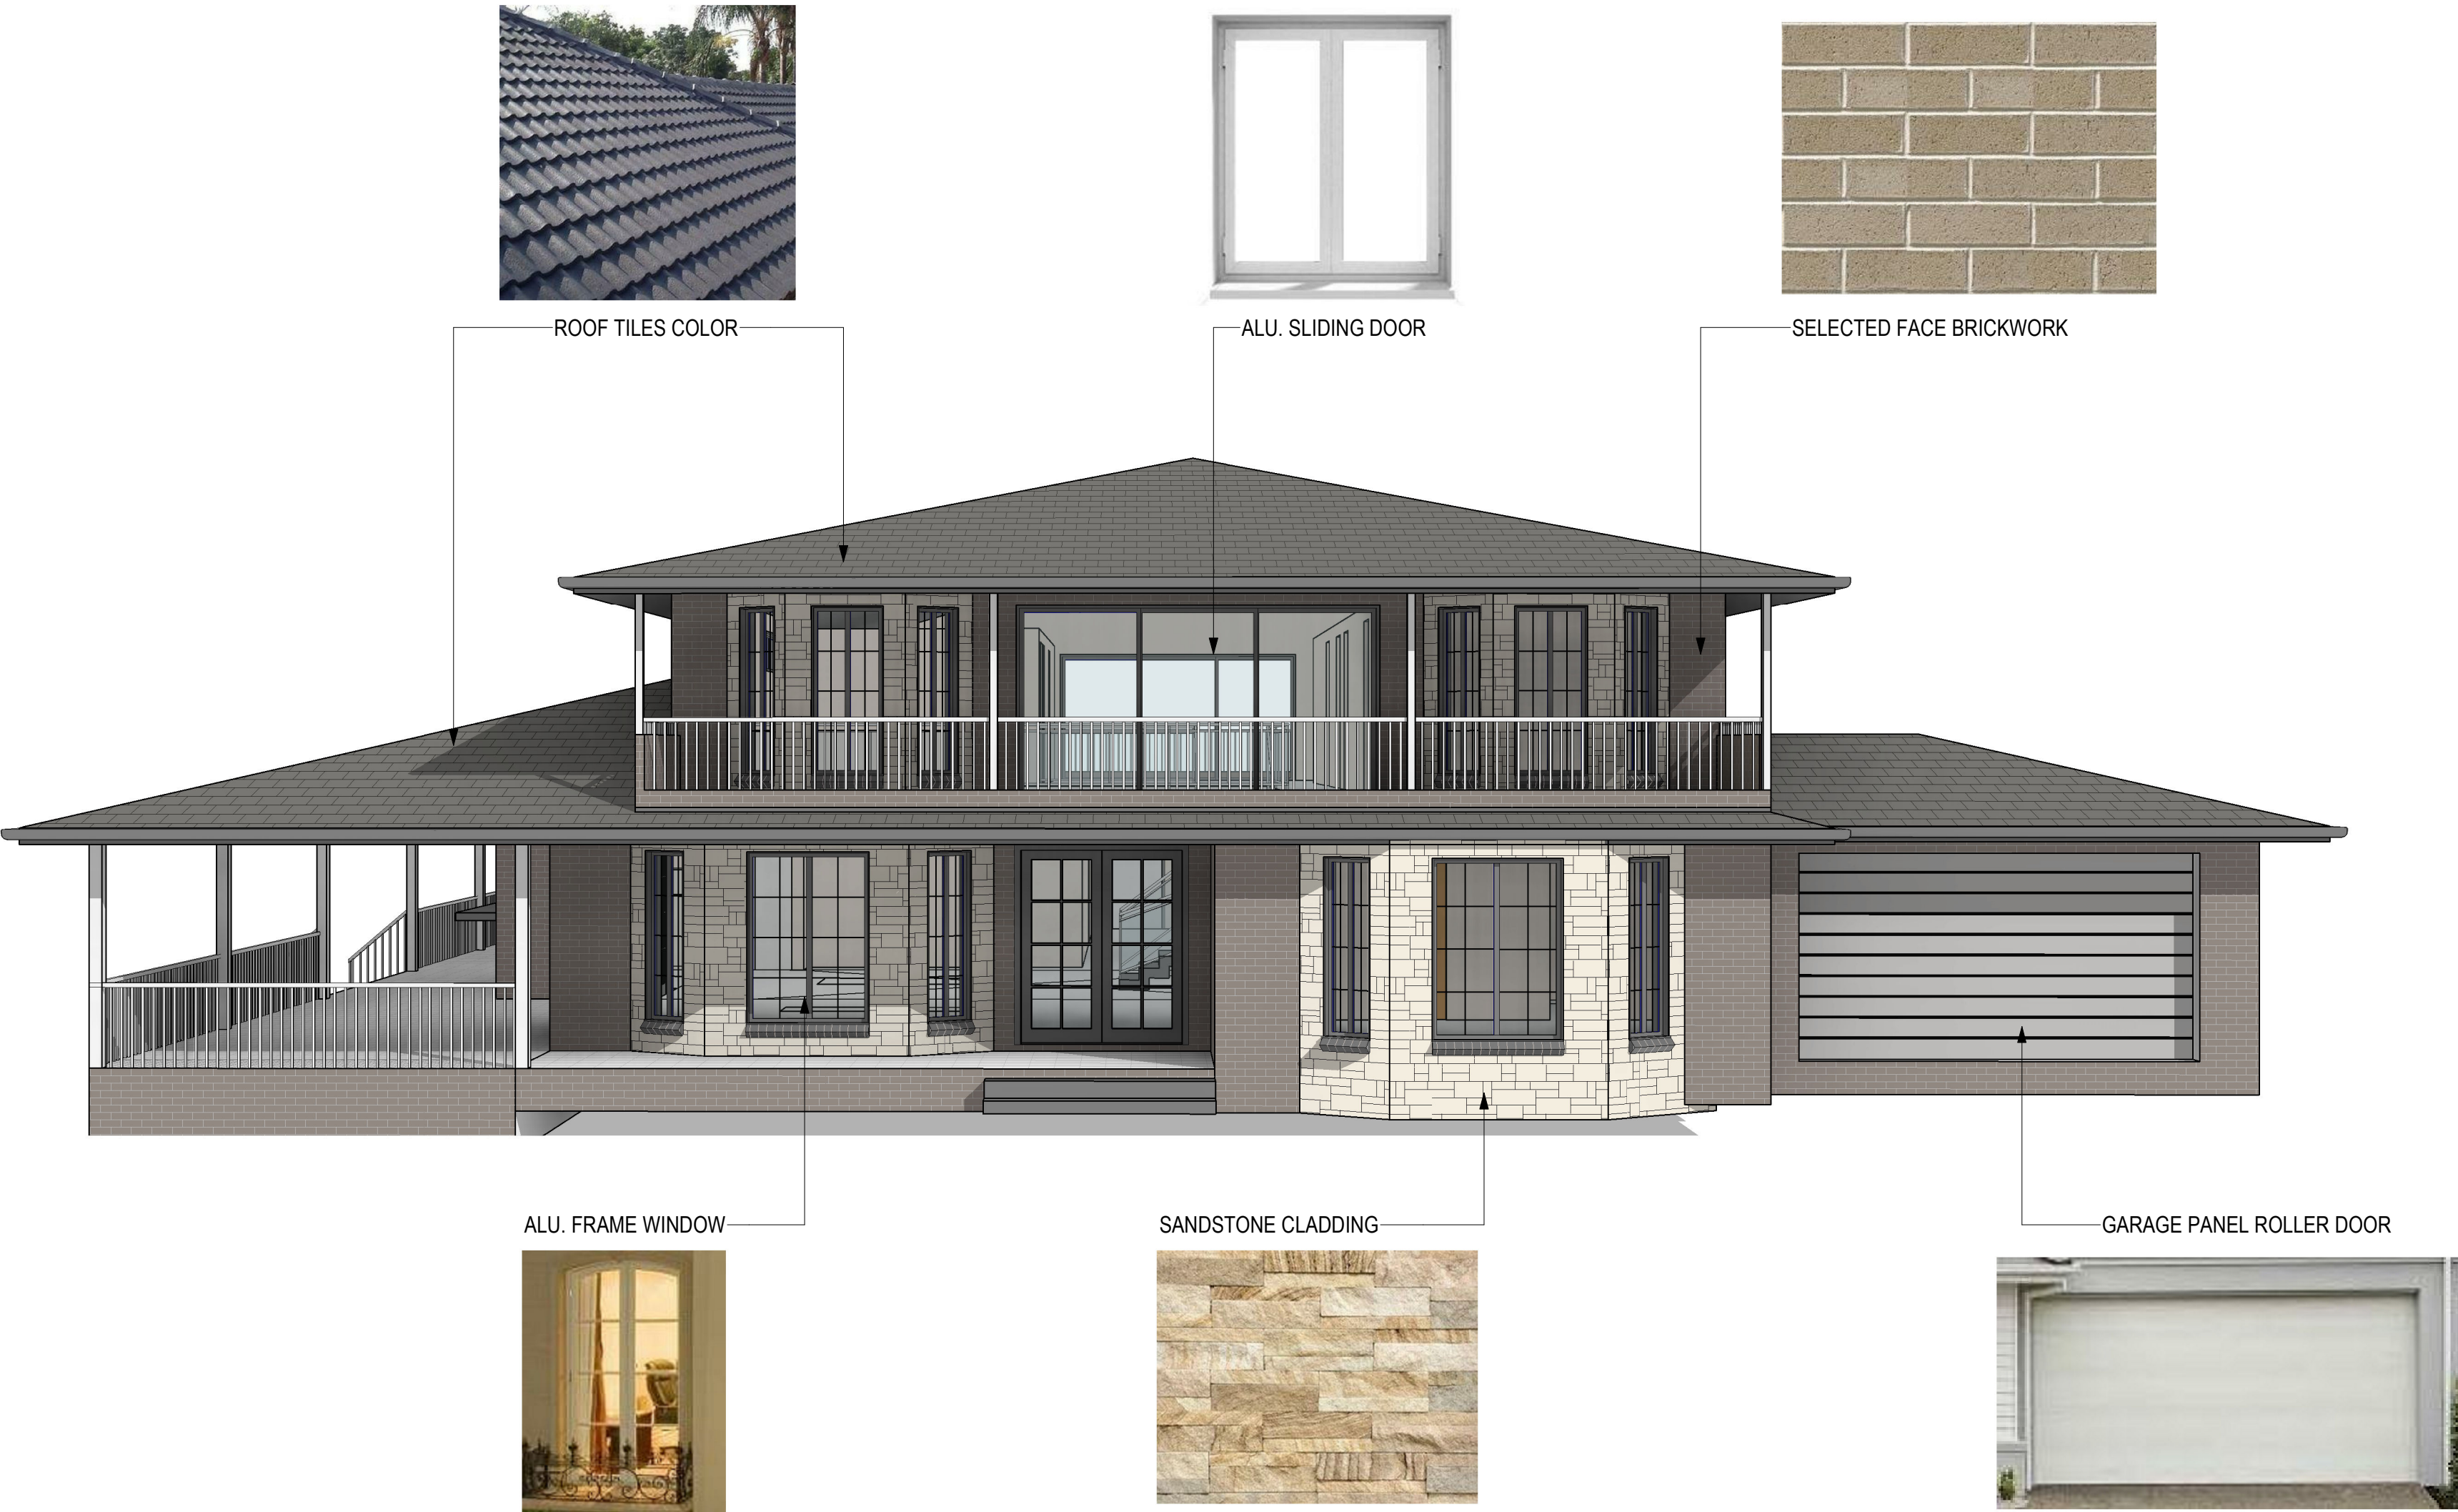

IMPORTANT CONSTRUCTION NOTES:

- REFER TO BCA REPORT FOR BUILDING REQUIREMENTS / PERFORMANCE SOLUTION / BUILDING UPGRADE.
- REFER TO FER REPORT PREAPRED BY FE CONSULTING P/L FOR PERFORMANCE SOLUTION / CONSTRUCTION UPGRADE.
- SITE AFFECTED BY BUSHFIRE PRONE, BAL 12.5 RATED MATERIALS MUST BE USED TO COMPLY WITH THE BUSHFIRE ASSESSMENT REPORT.

©THIS DRAWING IS THE PROPERTY OF LT DESIGN & CONSULTING PTY LTD AND WE RESERVE THE COPYRIGHT TO ALL OUR DESIGNS WHICH CANNOT BE REPRODUCED (IN PART OR IN WHOLE) BEFORE FIRST OBTAINING WRITTEN CONSENT. CONTRAVENTION WILL BE PROSECUTED

- FIGURED DIMENSIONS TO BE TAKEN IN PREFERENCE TO SCALE.
- BUILDERS' WORK TO COMPLY WITH THE LATEST BCA AND ITS AMENDMENTS AND RELEVANT AUSTRALIAN STANDARDS REFERRED WITHIN.

No.	Description	Date
1	REVISE AS PER COUNCIL REQUIREMENTS	22/03/2025



DESIGN

Building Design | 3D Modeling | Drafting | Detailing



BUILDING DESIGNERS AUSTRALIA

Accreditation No: 6302
Shop 6A/80 Thorneley Rd, Fairfield West
0414 891 998 - Le@LTDesign.net.au

DRAWING:

MATERIAL SCHEDULE OF FINISHES

CLIENT & PROJECT: LOT 1 IN DP 1033745

CONSTRUCTION CERTIFICATE FOR DOUBLE STOREY DWELLING AT NO.3 GILL AVENUE, AVOCA BEACH, NSW 2251

CONSTRUCTION CERTIFICATE

DATE: 22/03/2025


DWG NO: CC-10

SCALE:

DRW BY: LT

(A2)



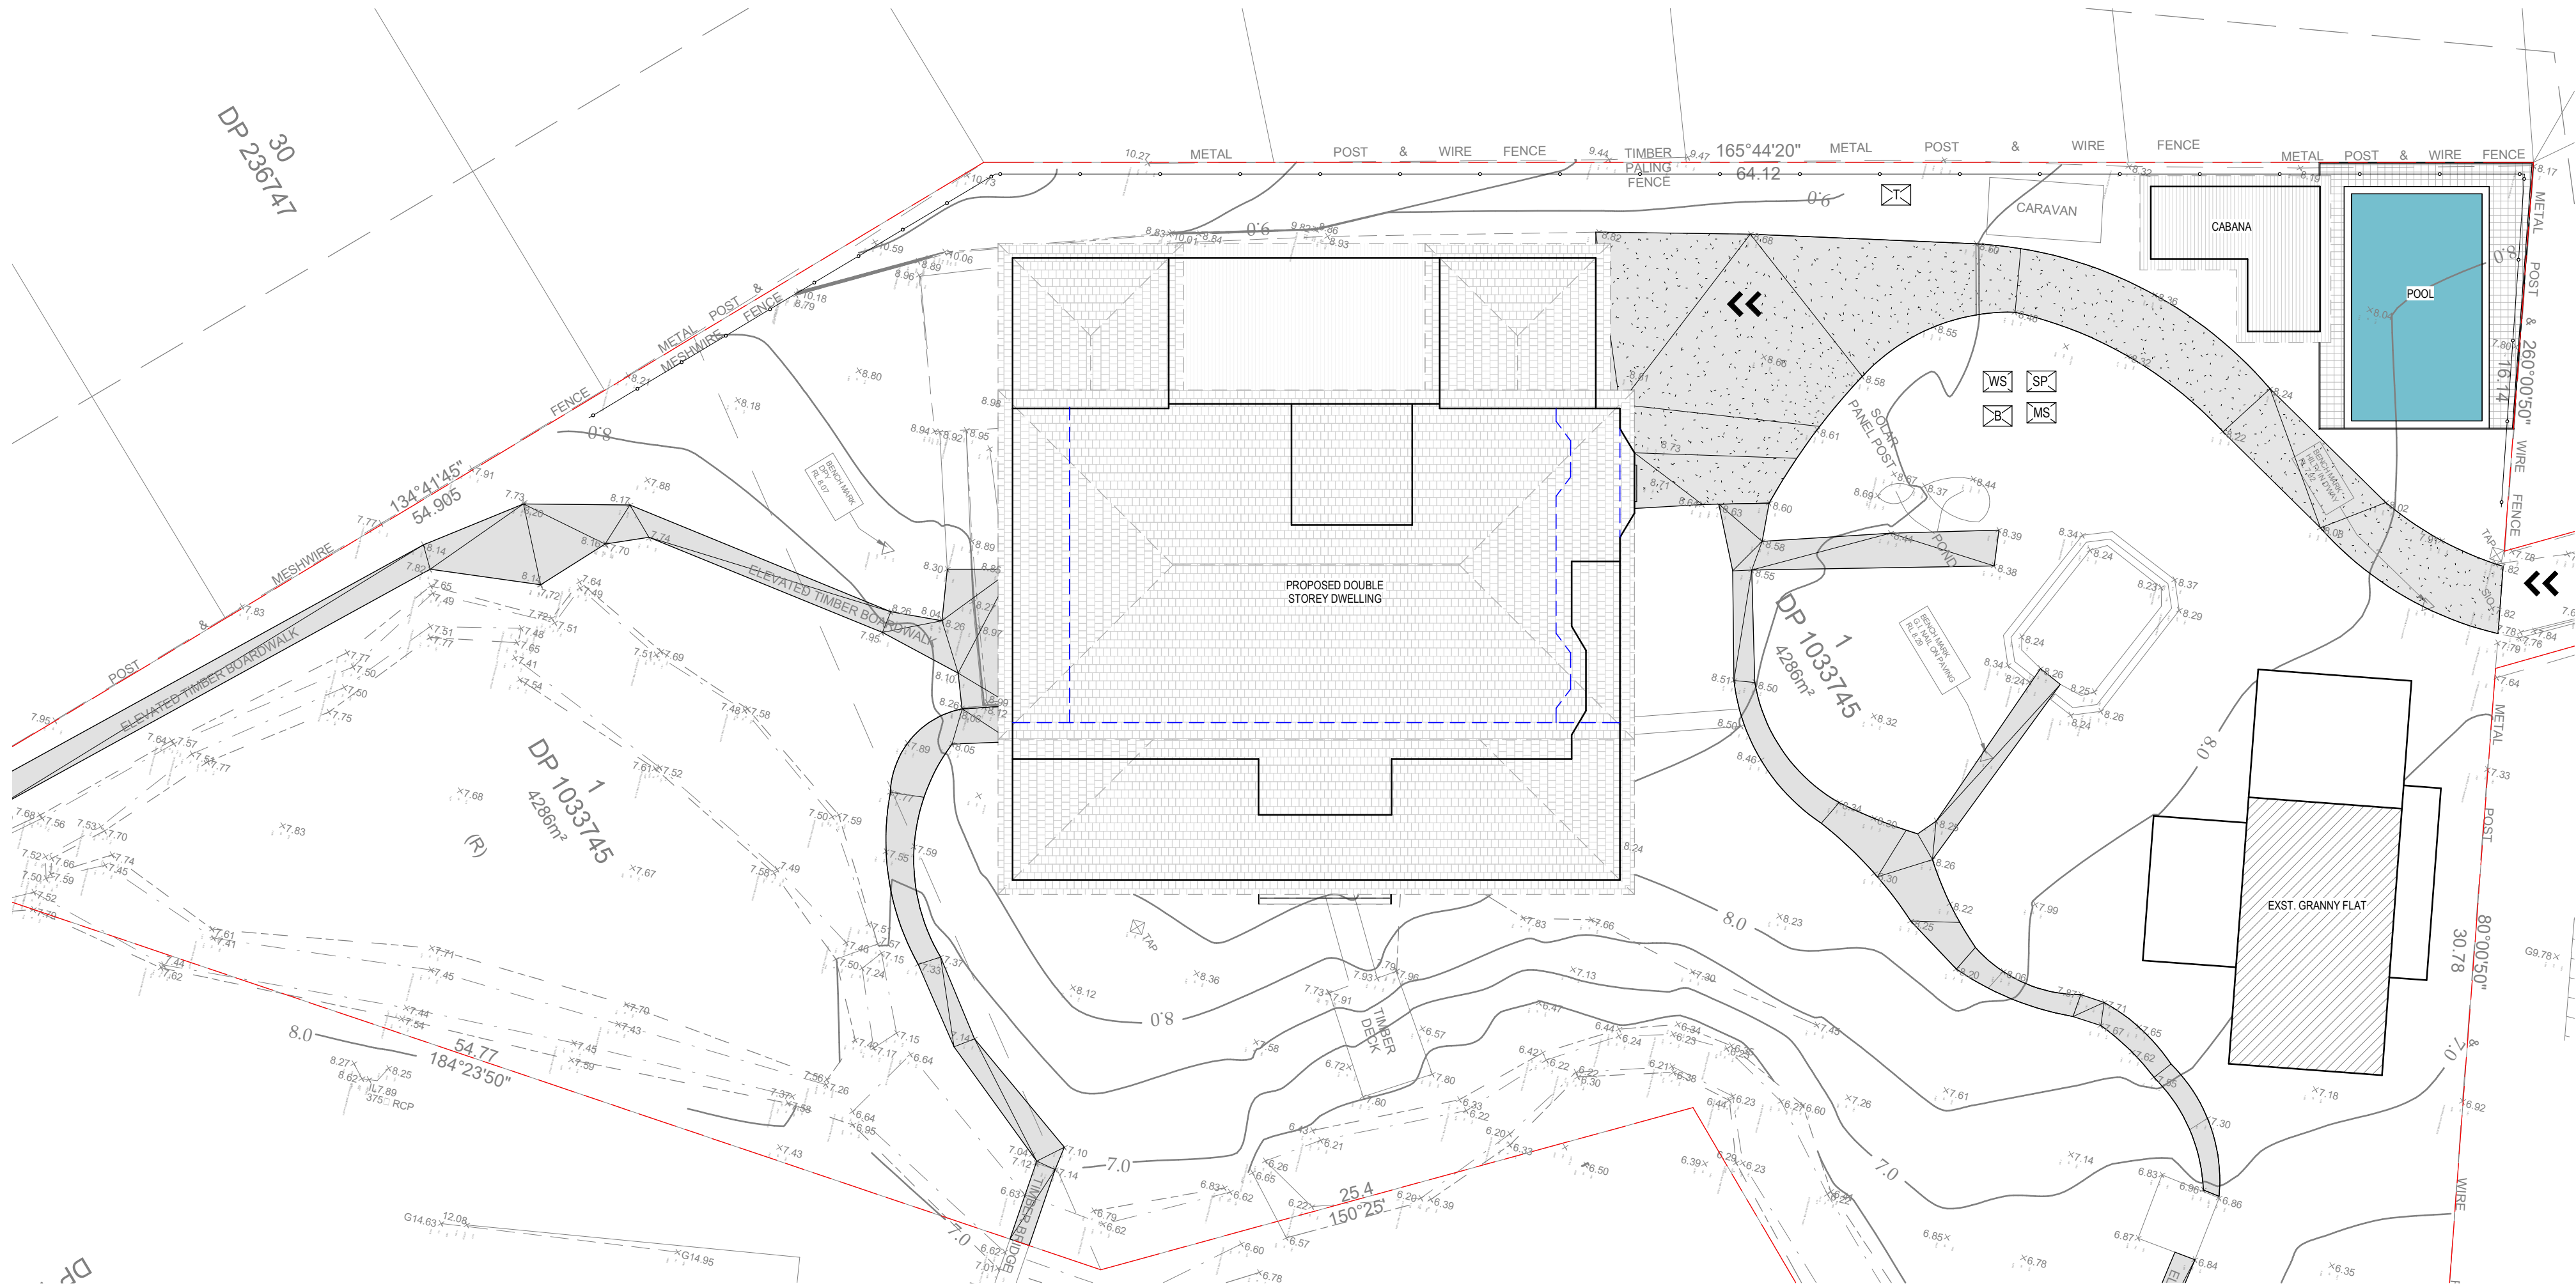

IMPORTANT CONSTRUCTION NOTES:

- REFER TO BCA REPORT FOR BUILDING REQUIREMENTS / PERFORMANCE SOLUTION / BUILDING UPGRADE.
- REFER TO FER REPORT PREPARED BY FE CONSULTING P/L FOR PERFORMANCE SOLUTION / CONSTRUCTION UPGRADE.
- SITE AFFECTED BY BUSHFIRE PRONE. BAL 12.5 RATED MATERIALS MUST BE USED TO COMPLY WITH THE BUSHFIRE ASSESSMENT REPORT.




1. NO VEHICLE CROSSING OR STOCKPILING OF MATERIAL SHOULD OCCUR ON THE VEGETATED BUFFER.
2. ALL SEDIMENT CONTROL STRUCTURES SHOULD BE INSPECTED & MAINTAINED BY THE SITE MANAGE DAILY
3. ALL SEDIMENT RETAINING STRUCTURES SHOULD BE CLEANED ON REACHING 50% STORAGE CAPACITY. SEDIMENT REMOVED SHOULD BE SPREAD WITHIN THE DISTURBED AREA.
4. ALL EXISTING VEGETATION ON THE SITE PERIMETER MUST BE RETAINED.
5. ROOF GUTTERS AND DOWNPIPES MUST BE CONNECT TO THE SITE DRAINAGE IMMEDIATELY AFTER ROOF CONSTRUCTION.
6. ALL DISTURBED AREA ARE TO BE RE-VEGETATED OR STABILISED TO PREVENT EROSION. I.E. LANDSCAPING/ MULCHING/ TURFING.
7. MATERIALS AREA NOT TO BE STORED ON THE FOOTPATH.

GENERAL LEGEND

- SILT FENCE
STOCKPILE
MATERIAL STORAGE
WASTE STORAGE & RECYCLING AREA
GARBAGE BIN
ONSITE TOILET
ACCESS FOR VEHICLES



① EROSION AND SEDIMENT CONTROL PLAN
1 : 200

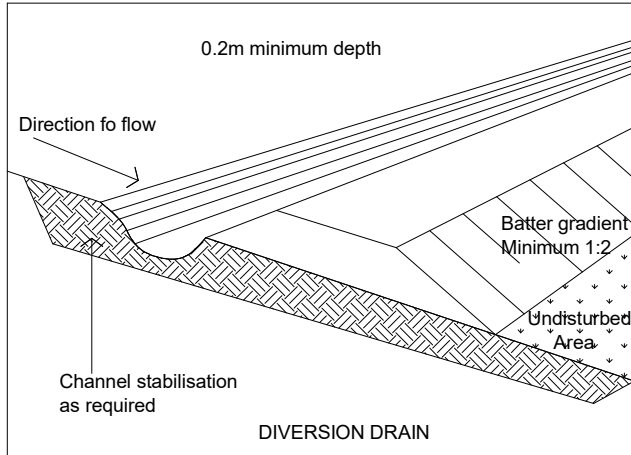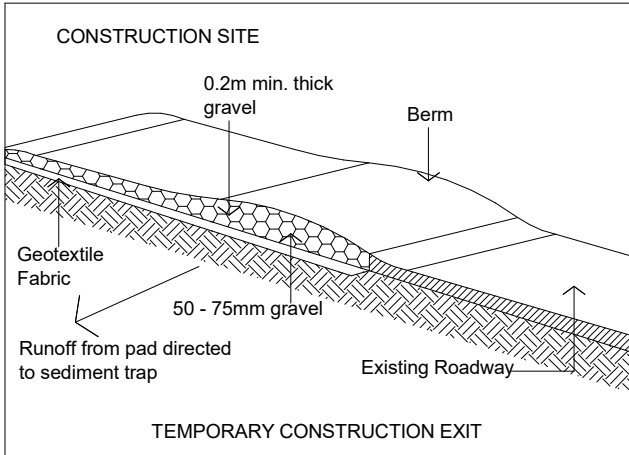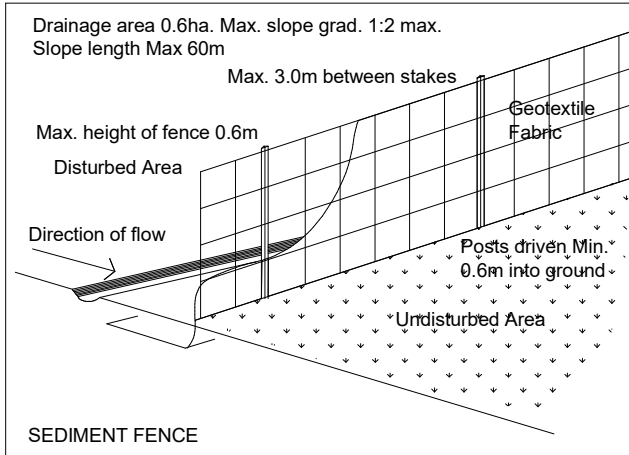

© THIS DRAWING IS THE PROPERTY OF LT DESIGN & CONSULTING PTY LTD AND WE RESERVE THE COPYRIGHT TO ALL OUR DESIGNS WHICH CANNOT BE REPRODUCED (IN PART OR IN WHOLE) BEFORE FIRST OBTAINING WRITTEN CONSENT. CONTRAVENTION WILL BE PROSECUTED

- FIGURED DIMENSIONS TO BE TAKEN IN PREFERENCE TO SCALE.
- BUILDERS' WORK TO COMPLY WITH THE LATEST BCA AND ITS AMENDMENTS AND RELEVANT AUSTRALIAN STANDARDS REFERRED WITHIN.

No.	Description	Date
1	REVISE AS PER COUNCIL REQUIREMENTS	22/03/2025






DRAWING:
EROSION AND SEDIMENT CONTROL PLAN

CLIENT & PROJECT: LOT 1 IN DP 1033745
CONSTRUCTION CERTIFICATE FOR DOUBLE STOREY DWELLING AT NO.3 GILL AVENUE, AVOCA BEACH, NSW 2251

DATE:
22/03/2025
DWG NO:
CC-11
DRW BY:
LT

SCALE:
As indicated (A2)


CONSTRUCTION CERTIFICATE

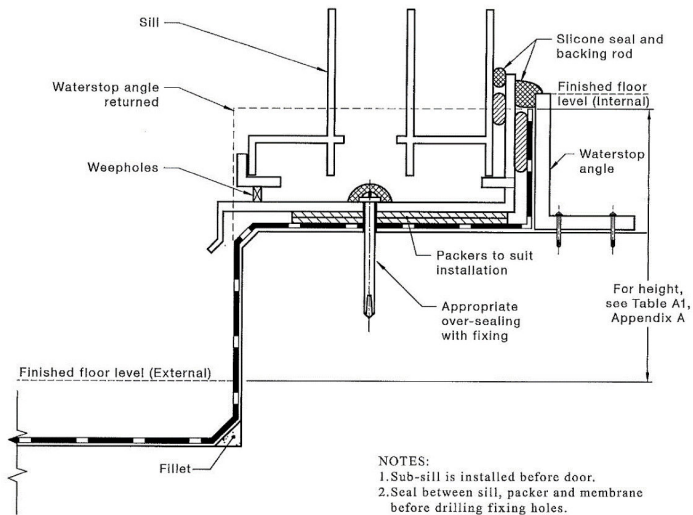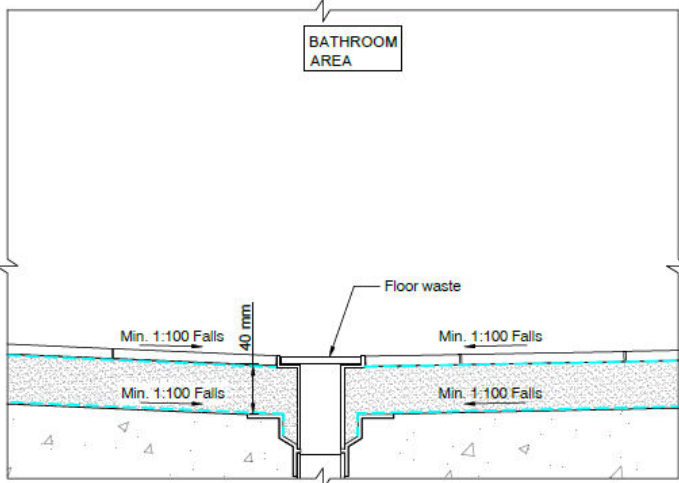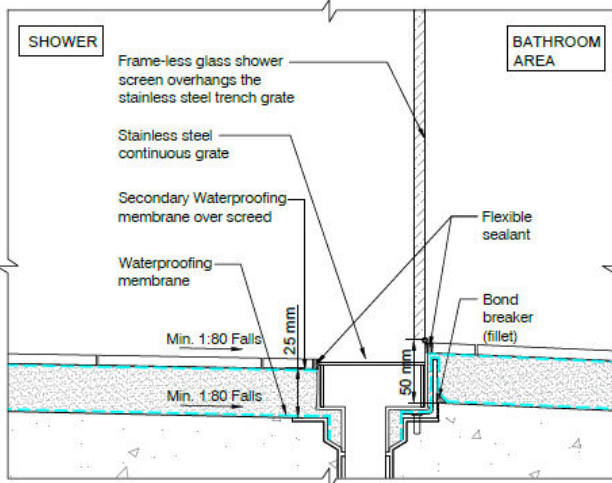

LEGEND:

- WATERPROOFING TO INTERNAL WET AREA AS PER AS 3740
- WATERPROOFING TO EXTERNAL WET AREA AS PER AS 4654 (BALCONIES ONLY)
- WATERPROOFING TO EXTERNAL WET AREA AS PER AS 4654
- WATERPROOFING TO PLANTER BOX

ALL FLOOR WASTES NEED TO INSTALL LEAK CONTROL FLANGES

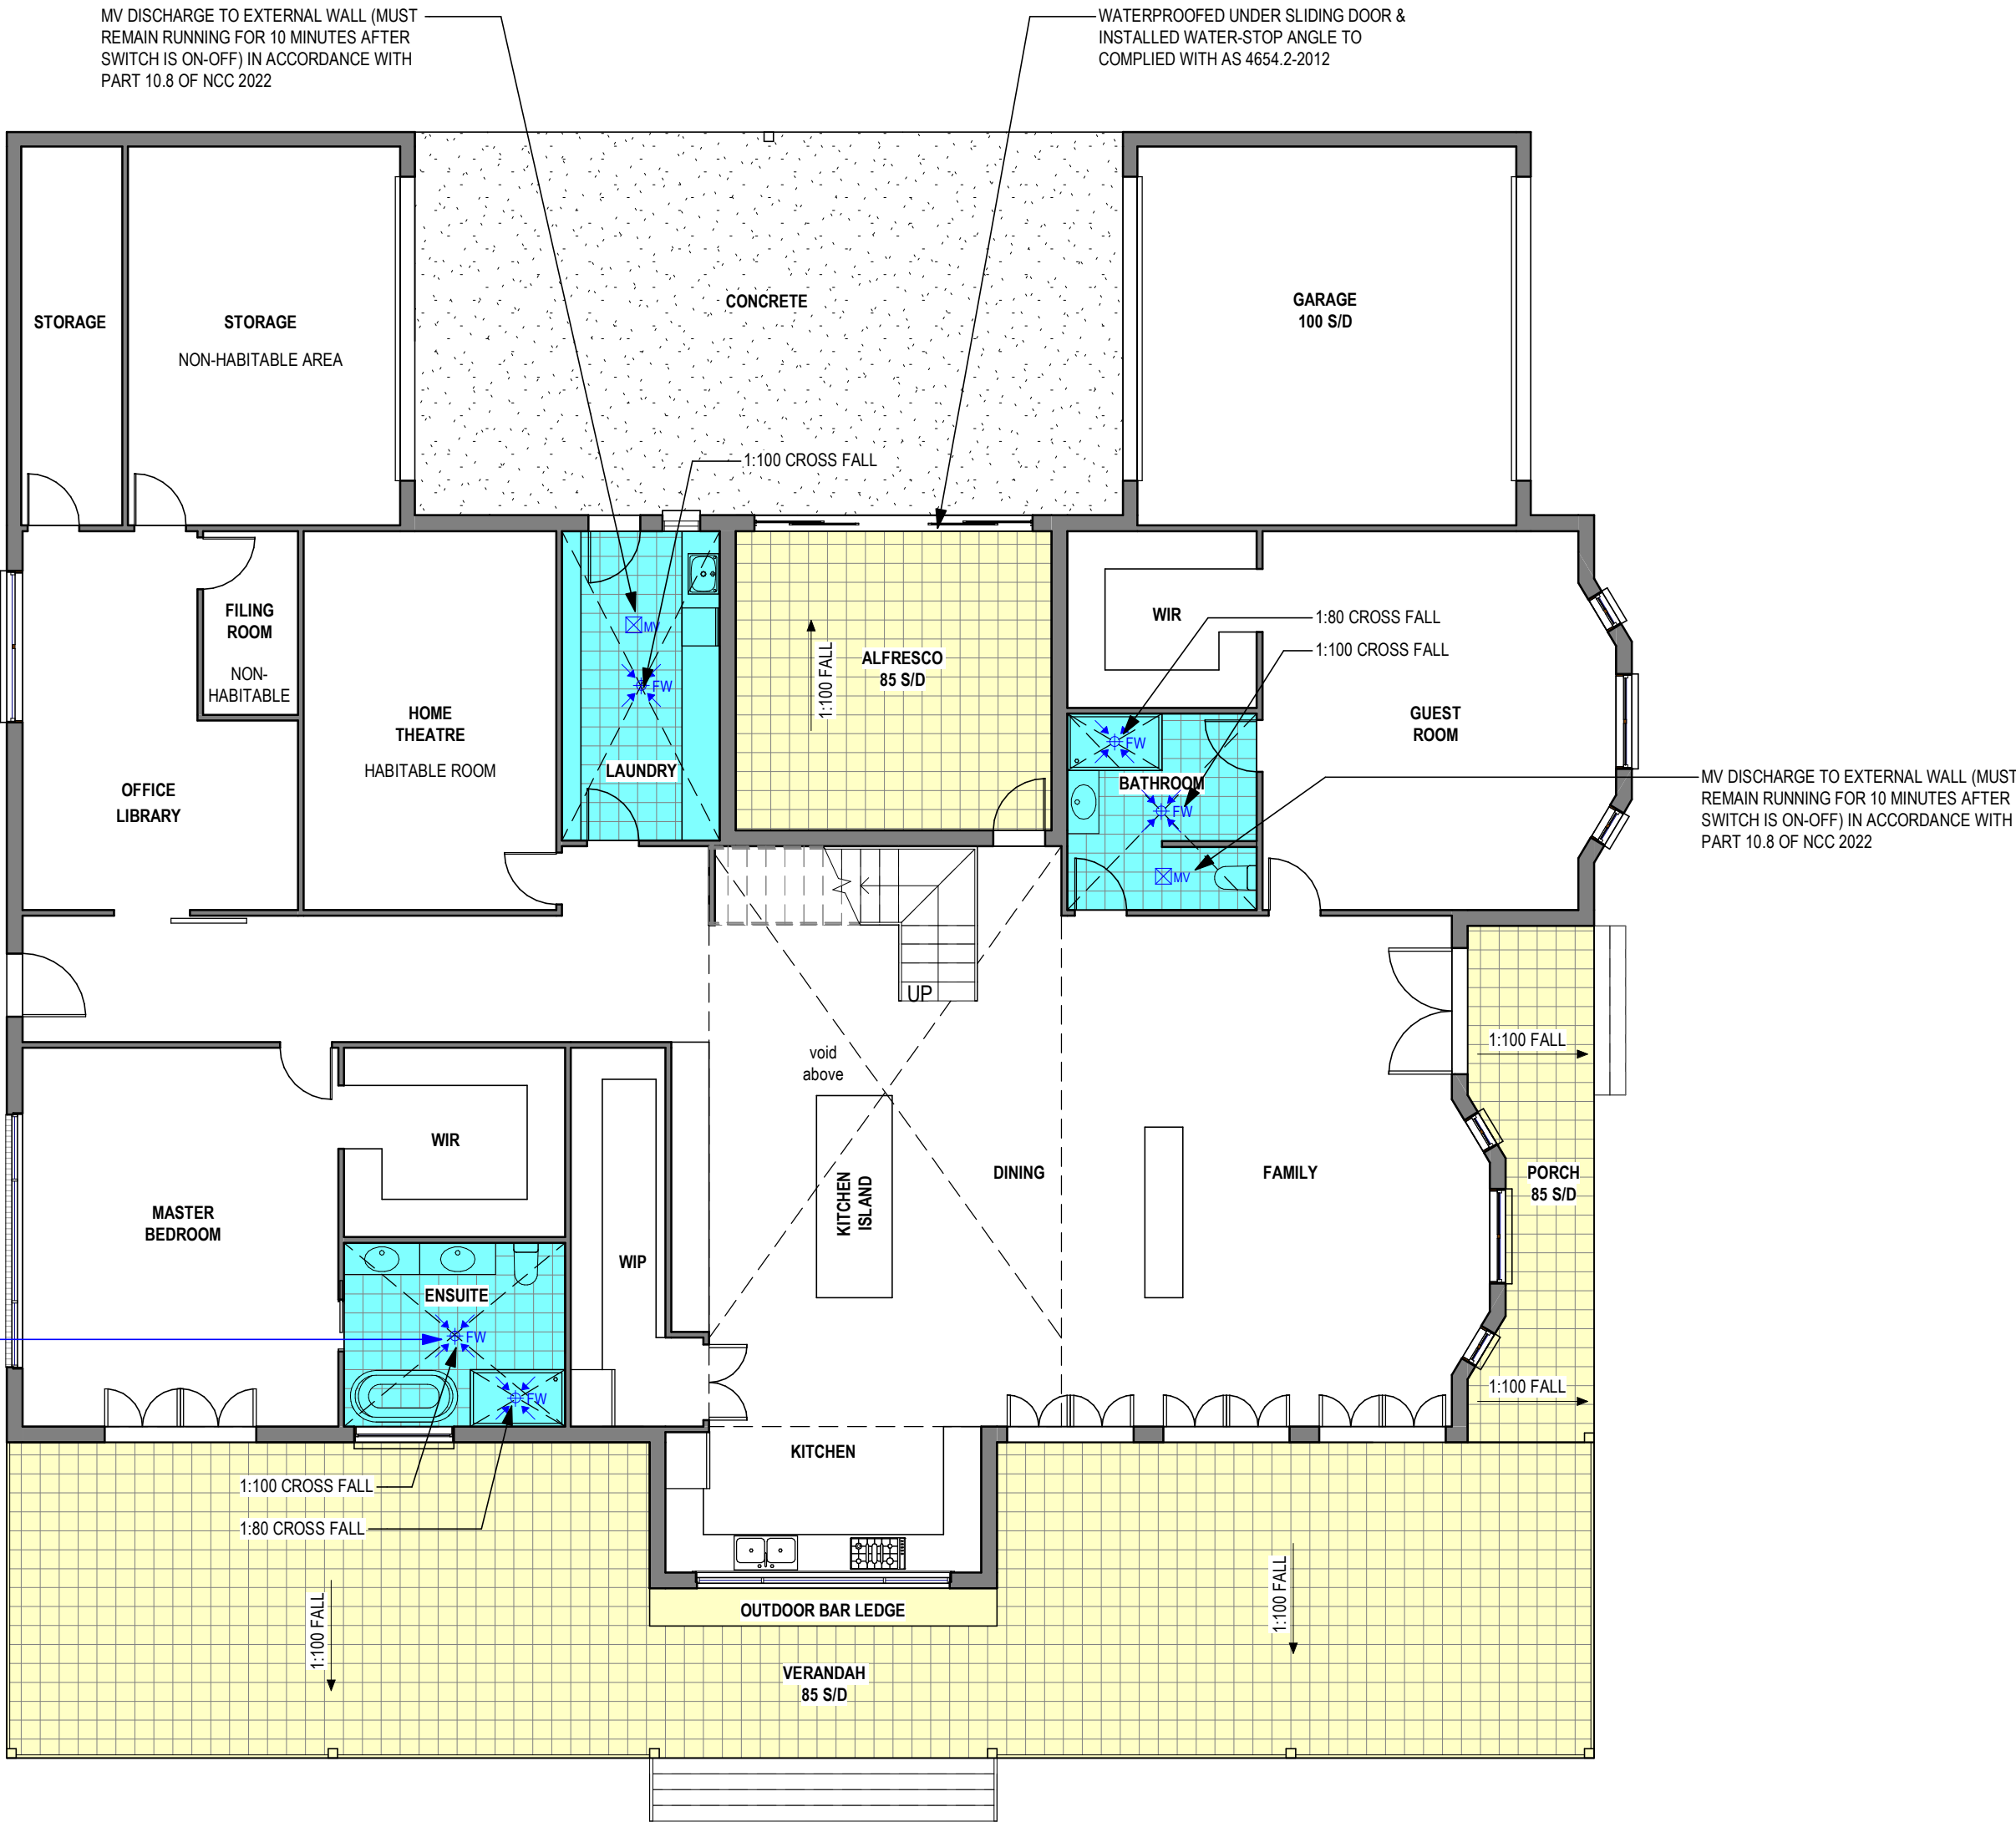

1 WET AREAS PLAN - GROUND FLOOR
1 : 100

© THIS DRAWING IS THE PROPERTY OF LT DESIGN & CONSULTING PTY LTD AND WE RESERVE THE COPYRIGHT TO ALL OUR DESIGNS WHICH CANNOT BE REPRODUCED (IN PART OR IN WHOLE) BEFORE FIRST OBTAINING WRITTEN CONSENT. CONTRAVENTION WILL BE PROSECUTED

• FIGURED DIMENSIONS TO BE TAKEN IN PREFERENCE TO SCALE.

• BUILDERS' WORK TO COMPLY WITH THE LATEST BCA AND ITS AMENDMENTS AND RELEVANT AUSTRALIAN STANDARDS REFERRED WITHIN.

No.	Description	Date
1	REVISE AS PER COUNCIL REQUIREMENTS	22/03/2025



Accreditation No: 6302
Shop 6A/80 Thorne Rd, Fairfield West
0414 891 998 - Le@LTDesign.net.au

Building Design | 3D Modeling | Drafting | Detailing

DRAWING:
WET AREAS PLAN - GROUND FLOOR

CLIENT & PROJECT: LOT 1 IN DP 1033745
CONSTRUCTION CERTIFICATE FOR DOUBLE STOREY DWELLING
AT NO.3 GILL AVENUE, AVOCA BEACH, NSW 2251


CONSTRUCTION CERTIFICATE

DATE:
22/03/2025
DWG NO:
CC-12






DRW BY:
LT

SCALE: 1 : 100 (A2)

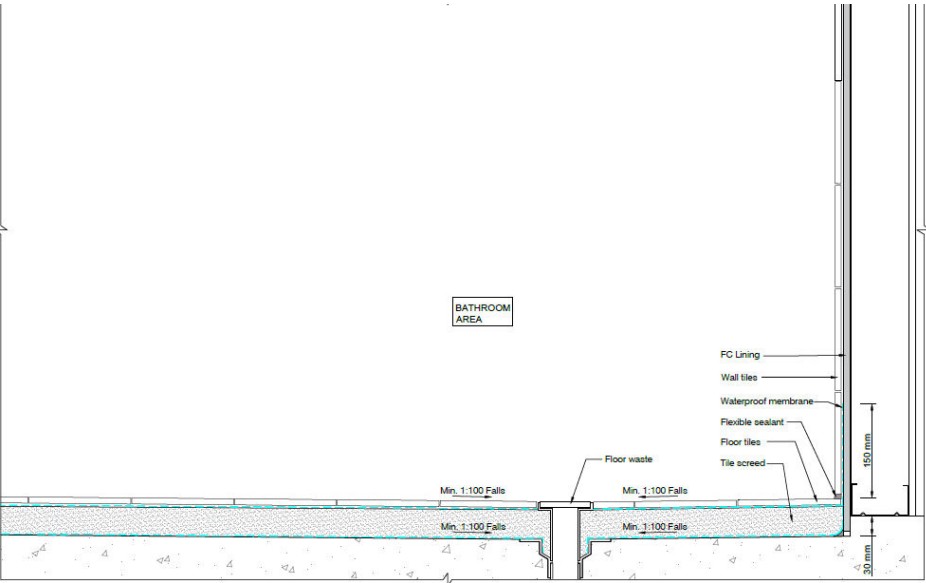




OVERFLOWS

The membrane must be turned into the overflow to prevent moisture from tracking behind the membrane.

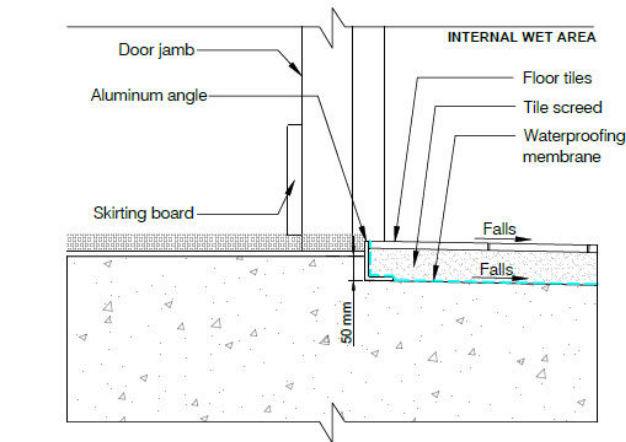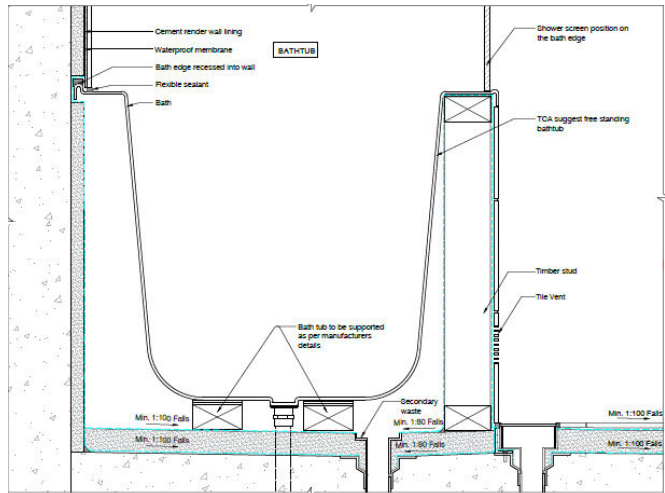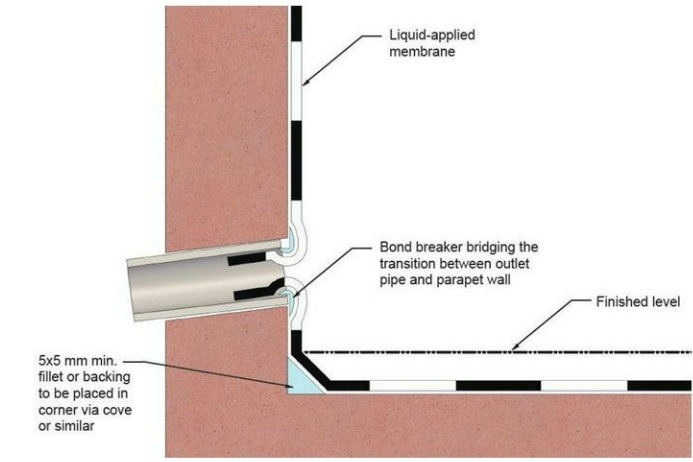

INTERNAL WET AREA DOOR THRESHOLD

LEGEND:

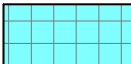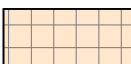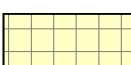-  WATERPROOFING TO INTERNAL WET AREA AS PER AS 3740
-  WATERPROOFING TO EXTERNAL WET AREA AS PER AS 4654 (BALCONIES ONLY)
-  WATERPROOFING TO EXTERNAL WET AREA AS PER AS 4654
-  WATERPROOFING TO PLANTER BOX

© THIS DRAWING IS THE PROPERTY OF LT DESIGN & CONSULTING PTY LTD AND WE RESERVE THE COPYRIGHT TO ALL OUR DESIGNS WHICH CANNOT BE REPRODUCED (IN PART OR IN WHOLE) BEFORE FIRST OBTAINING WRITTEN CONSENT. CONTRAVENTION WILL BE PROSECUTED

• FIGURED DIMENSIONS TO BE TAKEN IN PREFERENCE TO SCALE.

• BUILDERS' WORK TO COMPLY WITH THE LATEST BCA AND ITS AMENDMENTS AND RELEVANT AUSTRALIAN STANDARDS REFERRED WITHIN.

No.	Description	Date
1	REVISE AS PER COUNCIL REQUIREMENTS	22/03/2025



Building Design | 3D Modeling | Drafting | Detailing



Accreditation No: 6302
Shop 6A/80 Thorne Rd, Fairfield West
0414 891 998 - Le@LTDesign.net.au

DRAWING:

WET AREAS PLAN - FIRST FLOOR

CLIENT & PROJECT: LOT 1 IN DP 1033745

CONSTRUCTION CERTIFICATE FOR DOUBLE STOREY DWELLING
AT NO.3 GILL AVENUE, AVOCA BEACH, NSW 2251

CONSTRUCTION CERTIFICATE

DATE:
22/03/2025
DWG NO:
CC-13

DRW BY:
LT


SCALE: 1 : 100 (A2)




1 WET AREAS PLAN - FIRST FLOOR
1 : 100



NOTES:
ALL WATERPROOFING
MUST BE COMPLIED WITH:
- AS 3740:2021
- NCC 2022 - VOLUME 2 -
HOUSING PROVISIONS

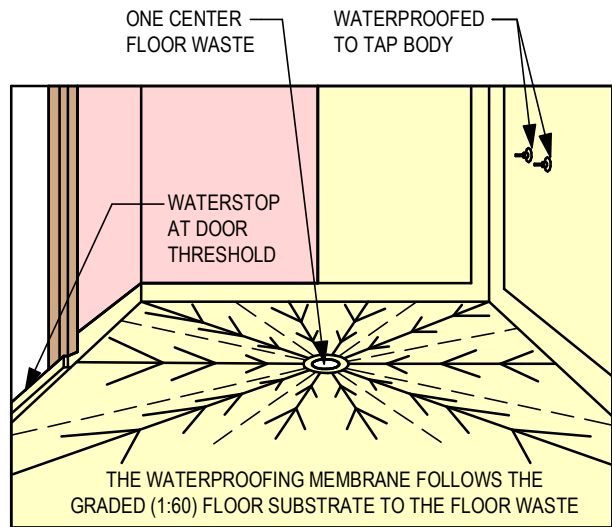

C01 CROSS FALL TO FLOOR WASTE

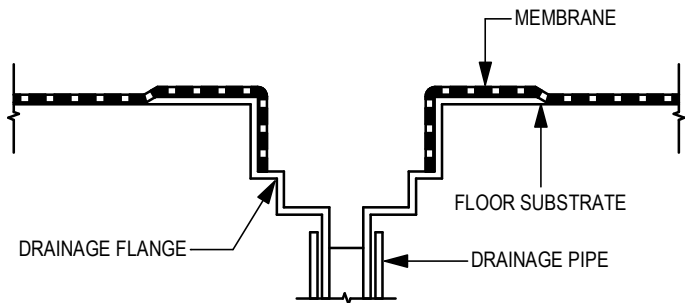


C02 TYPICAL MEMBRANE TERMINATION
AT DRAINAGE OUTLET
NOT TO SCALE




**PUDDLE / LEAK CONTROL
DRAINAGE FLANGES**


NOTE: MUST BE APPLIED TO ALL FLOOR WASTES IN WET AREA FOR
GROUND AND UPPER FLOOR / ENTIRE BUILDING
(CLASS 1 BUILDING: CONCRETE FLOOR - MAY SIT ON TOP OF
CONCRETE OR TILE BED FOR - CONCRETE FLOOR ONLY,
OTHER FLOORS - RECESSED INTO FLOOR SUBSTRATE OR TILE BED)

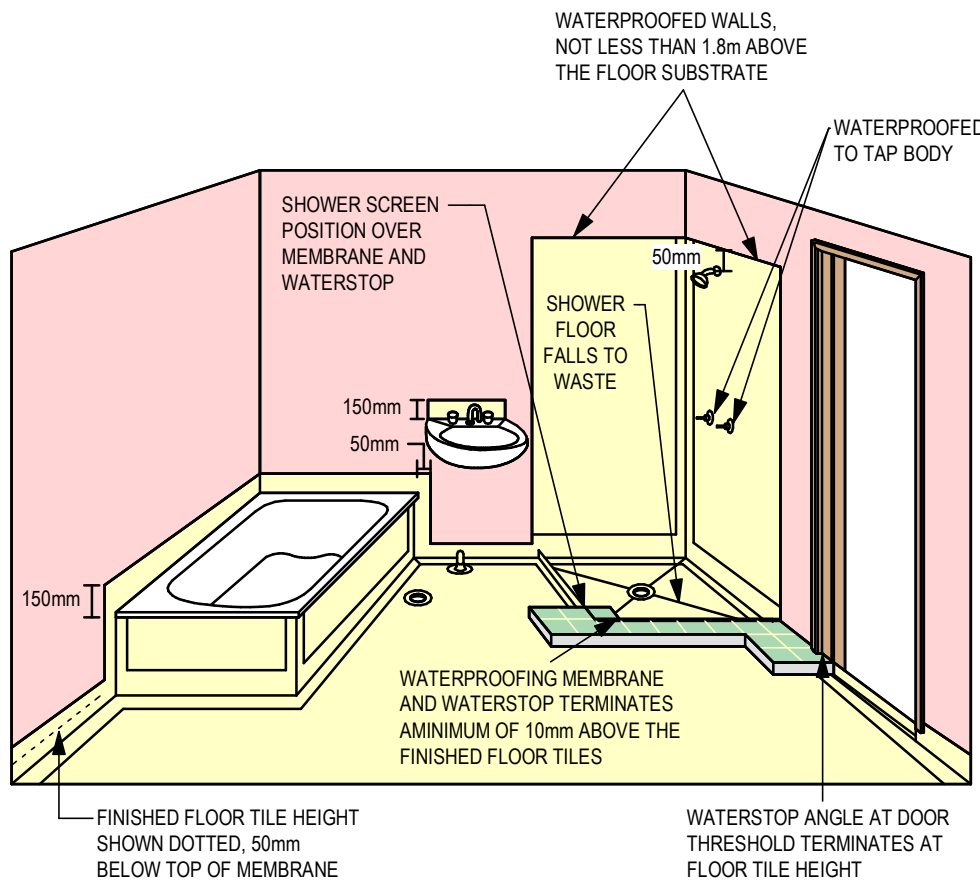

C03 WATERPROOFING DETAILS AROUND BATHROOM

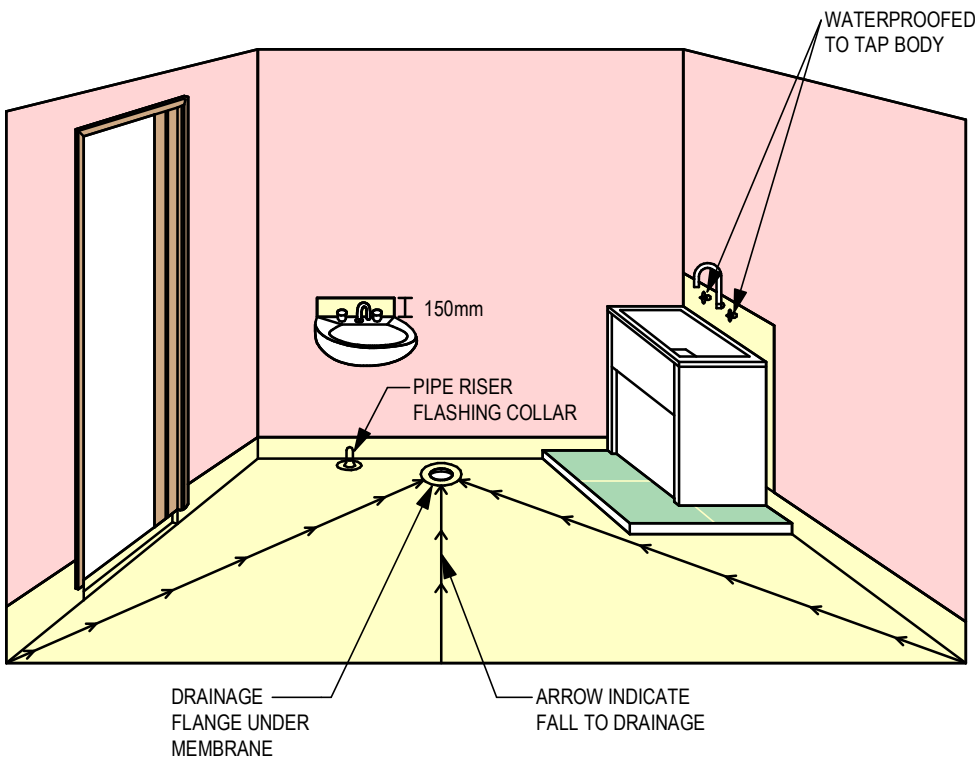

C04 WATERPROOFING DETAILS AROUND LAUNDRY

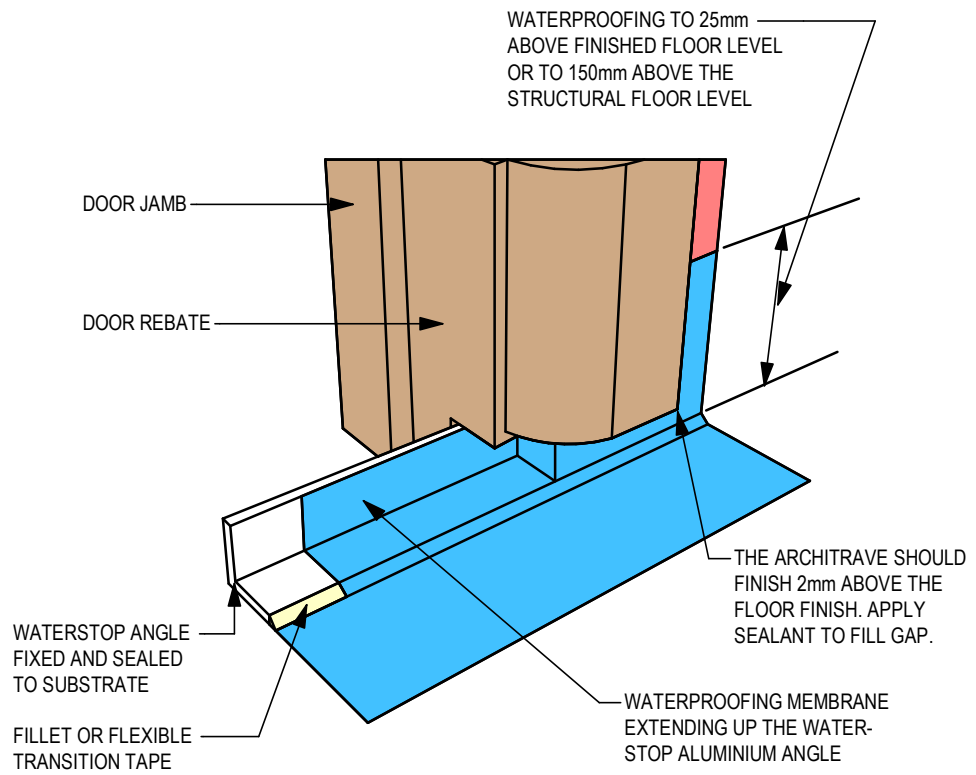

NOTE: THE WATERSTOP ANGLE MAY BE LOCATED AT
THE FACE OF THE DOOR JAMB OR AT THE REBATE.

C05 WATERPROOFING UNDER DOOR ARCHITRAVE

© THIS DRAWING IS THE PROPERTY OF LT DESIGN & CONSULTING PTY LTD AND WE RESERVE THE COPYRIGHT TO ALL OUR DESIGNS WHICH CANNOT BE REPRODUCED (IN PART OR IN WHOLE) BEFORE FIRST OBTAINING WRITTEN CONSENT. CONTRAVENTION WILL BE PROSECUTED

• FIGURED DIMENSIONS TO BE TAKEN IN PREFERENCE TO SCALE.

• BUILDERS' WORK TO COMPLY WITH THE LATEST BCA AND ITS AMENDMENTS AND RELEVANT AUSTRALIAN STANDARDS REFERRED WITHIN.

No.	Description	Date



Building Design | 3D Modeling | Drafting | Detailing



Accreditation No: 6302
Shop 6A/80 Thorne Rd, Fairfield West
0414 891 998 - Le@LTDesign.net.au

DRAWING:
TYPICAL WATERPROOFING CONSTRUCTION DETAILS

CLIENT & PROJECT: LOT 1 IN DP 1033745
**CONSTRUCTION CERTIFICATE FOR DOUBLE STOREY DWELLING
AT NO.3 GILL AVENUE, AVOCA BEACH, NSW 2251**

CONSTRUCTION CERTIFICATE

DATE:
22/03/2025
DWG NO:
CC-14

DRW BY:
LT

SCALE: 1 : 5 (A2)