

FOR CONSTRUCTION

LOT 25 IN DP 1289262
LOCATED AT NO.4 TRAVELLERS WAY TAHMOOR NSW 2573.

Proposed Construction of a New Single-Storey Residential Dwelling with Double Garage and Associated Site Works on a Vacant Allotment



OnBuild Certifiers Pty Ltd
Reference: 260036
Date: 27/07/2026
Andrew Soliman
Director/ Principal Certifier
GENERAL LEGEND
Consultant who prepared this document remains responsible for accuracy

BASIX COMMITMENTS		Certificate number: 1844136S Date of issue: Wednesday, 29 April 2026
WATER		
LANDSCAPE	162m2	
TOILETS	4 STARS	
KITCHEN TAPS	4 STARS	
SHOWER HEADS	4 STAR (>4.5 but <=6 Umin)	
BASIN TAPS	4 STARS	
ALTERNATIVE WATER	2000L RAINWATER TANK	
ROOF WATER TO TANK	261m2	
ALT.WATER USES- TANK	LAUNDRY	
ALT. WATER USES - RETIC	ALL TOILETS + ONE OUTDOOR TAP	
SWIMMING POOL	N/A	
ENERGY		
HOT WATER	GAS INSTANTANEOUS - 5 STAR	
AIR-CON (HEATING)	3 PHASE DUCTED - EER 3.0-3.5	
AIR-CON (COOLING)	3 PHASE DUCTED - EER 3.0-3.5	
VENTILATION - BATHROOM	NONE/ NATURAL VENTILATION	
VENTILATION - KITCHEN	DUCTED - MANUAL SWITCH	
VENTILATION - LAUNDRY	NONE/ NATURAL VENTILATION	
PV SYSTEM	N/A	
COOKTOP	GAS	
OVEN	ELECTRIC	
CLOTHES DRYING	OUTDOOR CLOTHESLINE	
LIGHTING	DEDICATED LED	

AL	ALUMINUM DOOR/ WINDOW
BAL	BALUSTRADE TYPE
BG	BOX GUTTER
BR1, BR2, etc.	BRICK FACE TYPE
CAP	METAL CAPPING
CD1, CD2, etc.	WALL CLADDING
CONC.	CONCRETE FLOOR
CPT	CARPET
CRT	CONCRETE ROOF TILES
CR1, CR2, etc.	CEMENT RENDER TYPE/ COLOUR
DPI/S	DOWN PIPE
DW	DISH WASHER
ED	ENTRY DOOR
F	FRIDGE
FAS	FASCIA
FET	FEATURE TILE
FT, FT1, FT2, etc.	FLOOR TILES
FW	FLOOR WASTE
GD	GARAGE DOOR
GUT	GUTTER
HWU	HOT WATER UNIT
HYB	HYBRID FLOOR
L	LINEN
MR	METAL ROOF
MW	MICROWAVE OVEN
NGL	NATURAL GROUND LEVEL
OBS	OBSURED GLASS
P	PANTRY
R	ROBE
RL	REDUCED LEVEL
RWH	RAIN WATER HEAD
RWT	RAIN WATER TANK
S	STORAGE
TOW	TOP OF WALL
TL	TIMBER LAMINATE
WC	WATER CLOSET
WM	WASHING MACHINE
SD	SMOKE DETECTOR

Sheet List 2				
Sheet Number	Sheet Name	Drawn By	Current Revision Date	Current Revision
CC.01	COVER SHEET	ROHIT	11-06-2026	CC ISSUE
CC.02A	GENERAL NOTES	ROHIT	11-06-2026	CC ISSUE
CC.02B	GENERAL NOTES	ROHIT		
CC.03	LOCATION PLAN AND SITE PLAN	ROHIT	11-06-2026	CC ISSUE
CC.04	CUT AND FILL PLAN	ROHIT	11-06-2026	CC ISSUE
CC.05	SITE ANALYSIS AND SEDIMENT CONTROL	ROHIT	11-06-2026	CC ISSUE
CC.06	GROUND FLOOR PLAN	ROHIT	11-06-2026	CC ISSUE
CC.07	ROOF PLAN	ROHIT	11-06-2026	CC ISSUE
CC.08	ELEVATION 01	ROHIT	11-06-2026	CC ISSUE

Sheet List 2				
Sheet Number	Sheet Name	Drawn By	Current Revision Date	Current Revision
CC.09	ELEVATION 02	ROHIT	11-06-2026	CC ISSUE
CC.10	SECTIONS	ROHIT	11-06-2026	CC ISSUE
CC.11	FLOOR AREA PLAN	ROHIT	11-06-2026	CC ISSUE
CC.12	RENTABLE AREA PLAN	ROHIT	11-06-2026	CC ISSUE
CC.13	COLOR SCHEDULE	ROHIT	11-06-2026	CC ISSUE
CC.14	LANDSCAPE PLAN	ROHIT	11-06-2026	CC ISSUE
CC.15	DRIVEWAY DETAILS	ROHIT		
CC.16	WATERPROOFING DETAILS	ROHIT	11-06-2026	CC ISSUE

NOTE: ALL IMAGES ARE FOR ILLUSTRATION ONLY AND ARE SUBJECT TO VARIATION AND TO AVAILABILITY OF MATERIALS.

1	11-06-2026	CC ISSUE	
REV	DATE	DESCRIPTION	BY



THIS DRAWING IS THE EXCLUSIVE PROPERTY OF THE DEVELOPER & THE REPRODUCTION OF ANY PART WITHOUT THE PRIOR WRITTEN CONSENT OF THE DEVELOPER IS A VIOLATION OF APPLICABLE LAWS. IN NO EVENT SHALL THE DEVELOPER BE HELD LIABLE FOR SPECIAL, COLLATERAL, INCIDENTAL OR CONSEQUENTIAL LIABILITY IN CONNECTION WITH THE USE OF THIS DIGITAL DATA ONCE RELEASED FROM THE DEVELOPER'S OFFICE. THIS DRAWING IS TO BE READ & UNDERSTOOD IN CONJUNCTION WITH THE STRUCTURAL, MECHANICAL, ELECTRICAL &/OR ANY OTHER CONSULTANT'S DOCUMENTATION AS MAY BE APPLICABLE TO THE PROJECT PRIOR TO THE START OF ANY WORKS AND FOR ITS DURATION.

PROJECT:
4 TRAVELLERS WAY
LOT 25 IN DP 1289262
No.04 TRAVELLERS WAYS
TAHMOOR nsw

DRAWING TITLE:
COVER SHEET

NORTH:

LOT NO:
25

DRAWN BY:
ROHIT

DATE:
1-07-2026

CHECKED BY:
RH

SCALE:
As indicated

DRAWING No:
CC.01

REV:
1

ISSUED BY:

CLIENT NAME:
Sudip Shreshta and Sanu Laxmi shreshta

BUILDING SPECIFICATIONS

National Construction Code – Volume 2, Amendment 1 – Building Code of Australia 2022 & Housing Provisions Standard 2022

SITE PREPARATION

- PART 3.1 OF THE NCC VOLUME 2, AMENDMENT 1 - BUILDING CODE OF AUSTRALIA 2022 & HOUSING PROVISIONS STANDARD 2022.

EARTHWORKS

- TO BE CARRIED OUT IN ACCORDANCE WITH THE REQUIREMENTS OF THE ENVIRONMENTAL PLANNING & ASSESSMENT ACT 1979 AND DEVELOPMENT CONSENT CONDITIONS
- PART 3.2 OF THE NCC VOLUME 2, AMENDMENT 1 - BUILDING CODE OF AUSTRALIA 2022 & HOUSING PROVISIONS STANDARD 2022.
- AS 4678:2002 - EARTH-RETAINING STRUCTURES

DRAINAGE

- PART 3.3 OF THE NCC VOLUME 2, AMENDMENT 1 - BUILDING CODE OF AUSTRALIA 2022 & HOUSING PROVISIONS STANDARD 2022.
- AS/NZS 3500.1:2021 - PLUMBING & DRAINAGE - WATER SERVICES
- AS/NZS 3500.2:2021 - PLUMBING & DRAINAGE - SANITARY PLUMBING & DRAINAGE
- AS/NZS 3500.3:2021 - PLUMBING & DRAINAGE STORMWATER DRAINAGE
- AS/NZS 3500.4:2021 - PLUMBING & DRAINAGE - HEATED WATER SERVICES

STRUCTURAL WORK

- Part 2.2 OF THE NCC VOLUME 2, AMENDMENT 1 - BUILDING CODE OF AUSTRALIA 2022 & HOUSING PROVISIONS STANDARD 2022.
- AS 4100:2020 - STEEL STRUCTURES CODES
- AS/NZS 1170.0:2002 - GENERAL PRINCIPLES
- AS/NZS 1170.1:2002 - PARTS 1 PERMANENT, IMPOSED AND OTHER ACTIONS
- AS/NZS 1170.2:2021 - PART 2 WIND ACTIONS
- AS 3700:2018 - SAA MASONRY CODE
- AS 1684.3:2021 - RESIDENTIAL TIMBER FRAMED CONSTRUCTION

FOOTINGS & SLABS

- PART 4 OF THE NCC VOLUME 2, AMENDMENT 1 - BUILDING CODE OF AUSTRALIA 2022 & HOUSING PROVISIONS STANDARD 2022.
- AS 2159:2009 - PILING - DESIGN & INSTALLATION
- AS 2870:2011 - RESIDENTIAL SLABS & FOOTINGS
- AS 3600:2018 - CONCRETE STRUCTURES

MASONRY

- PART 5 OF THE NCC VOLUME 2, AMENDMENT 1 - BUILDING CODE OF AUSTRALIA 2022 & HOUSING PROVISIONS STANDARD 2022.
- AS 3700:2018 - MASONRY STRUCTURES

FRAMING

- PART 6 OF THE NCC VOLUME 2, AMENDMENT 1 - BUILDING CODE OF AUSTRALIA 2022 & HOUSING PROVISIONS STANDARD 2022.
- AS 1684.2:2021 - RESIDENTIAL TIMBER-FRAMED CONSTRUCTION - NON- CYCLONIC AREAS
- AS 1720.1:2010 - TIMBER STRUCTURES - DESIGN METHODS
- AS 4100:2020 - STEEL STRUCTURES
- AS 3660.1:2014 - TERMITE MANAGEMENT SYSTEM

ROOF & WALL CLADDING

- PART 7 OF THE NCC VOLUME 2, AMENDMENT 1 - BUILDING CODE OF AUSTRALIA 2022 & HOUSING PROVISIONS STANDARD 2022.
- AS 1273:1991 - UNPLASTICIZED PVC (UPVC) DOWNPIPES & FITTINGS FOR RAINWATER
- AS 1562.1:2018 - DESIGN & INSTALLATION OF SHEET ROOF & WALL CLADDING - METAL
- AS/NZS 1562.3:2006 - DESIGN & INSTALLATION OF SHEET ROOF & WALL CLADDING - PLASTIC
- AS 2049:2002 - ROOF TILES
- AS 2050:2018 - INSTALLATION OF ROOF TILES
- AS 4285:2019 - ROOFLIGHTS

GLAZING

- PART 8 OF THE NCC VOLUME 2, AMENDMENT 1 - BUILDING CODE OF AUSTRALIA 2022 & HOUSING PROVISIONS STANDARD 2022.
- AS 1288:2021 - GLASS IN BUILDINGS - SELECTION & INSTALLATION
- AS 2047:2014 - WINDOWS & EXTERNAL GLAZED DOORS IN BUILDINGS
- AS/NZS 2208:1996 - SAFETY GLAZING MATERIALS IN BUILDINGS

FIRE SAFETY

- PART 9 OF THE NCC VOLUME 2, AMENDMENT 1 - BUILDING CODE OF AUSTRALIA 2022 & HOUSING PROVISIONS STANDARD 2022.
- AS 3786:2014 - SMOKE ALARMS USING SCATTERED LIGHT, TRANSMITTED LIGHT OR IONIZATION

HEALTH & AMENITY

- PART 10 OF THE NCC VOLUME 2, AMENDMENT 1 - BUILDING CODE OF AUSTRALIA 2022 & HOUSING PROVISIONS STANDARD 2022.
- AS/NZS ISO 717.1:2004 - ACOUSTICS - RATING OF SOUND INSULATION IN BUILDINGS & OF BUILDING ELEMENTS - AIRBORNE SOUND INSULATION
- AS ISO 717.2:2004 - ACOUSTICS - RATING OF SOUND INSULATION IN BUILDINGS & OF BUILDING ELEMENTS - IMPACT SOUND INSULATION
- AS 1668.2:2012 - THE USE OF VENTILATION & AIR CONDITIONING IN BUILDINGS - MECHANICAL VENTILATION IN BUILDINGS
- AS 1668.4:2012 - THE USE OF VENTILATION & AIR CONDITIONING IN BUILDINGS - NATURAL VENTILATION OF BUILDINGS
- AS/NZS 1680.0:2009 - INTERIOR LIGHTING - SAFE MOVEMENT
- AS 3740:2021 - WATERPROOFING OF DOMESTIC WET AREAS
- AS 3000:2018 - ELECTRICAL INSTALLATION
- BCA Part 10.8.1, AS4200.1 & AS4200.2 - PLIABLE BUILDING MEMBRANE INSTALLED.

WATERPROOFING

- PART 10.2 OF THE NCC VOLUME 2, AMENDMENT 1 - BUILDING CODE OF AUSTRALIA 2022 & HOUSING PROVISIONS STANDARD 2022
- AS 3740:2021 - WATERPROOFING TO WET AREA
- AS 4654:2012 - EXTERNAL WET AREAS

SAFE MOVEMENT & ACCESS

- PART 11 OF THE NCC VOLUME 2, AMENDMENT 1 - BUILDING CODE OF AUSTRALIA 2022 & HOUSING PROVISIONS STANDARD 2022.
- AS 1428.1:2009 - DESIGN FOR ACCESS & MOBILITY - GENERAL REQUIREMENTS FOR ACCESS - NEW BUILDING WORK
- AS 1657:2018 - FIXED PLATFORMS, WALKWAYS, STAIRWAYS & LADDERS - DESIGN, CONSTRUCTION & INSTALLATION

OnBuild Certifiers Pty Ltd
Handrails & Balustrade: 260036
PART 11.3.3 OF THE NCC VOLUME 2, AMENDMENT 1 - BUILDING CODE OF AUSTRALIA 2022 & HOUSING PROVISIONS STANDARD 2022.
PART 11.3.4 OF THE NCC VOLUME 2, AMENDMENT 1 - BUILDING CODE OF AUSTRALIA 2022 & HOUSING PROVISIONS STANDARD 2022.
PART 11.3.5 OF THE NCC VOLUME 2, AMENDMENT 1 - BUILDING CODE OF AUSTRALIA 2022 & HOUSING PROVISIONS STANDARD 2022.
AS 1170.1:2002 - BALUSTRADE INSTALLATION

PROTECTION OF OPENABLE WINDOW

- PART 11.3.7 AND 11.3.8 OF THE NCC VOLUME 2, AMENDMENT 1 - BUILDING CODE OF AUSTRALIA 2022 & HOUSING PROVISIONS STANDARD 2022.

ENERGY EFFICIENCY

- PART 13 OF THE NCC VOLUME 2, AMENDMENT 1 - BUILDING CODE OF AUSTRALIA 2022 & HOUSING PROVISIONS STANDARD 2022 & BASIX CERTIFICATE.

MECHANICAL VENTILATION

- EXHAUST FROM A BATHROOM, SANITARY COMPARTMENT TO DISCHARGE DIRECTLY TO OUTDOOR AIR WITH MINIMUM FLOW RATE OF 25L/S & MAKE-UP AIR VIA OPENINGS TO AN ADJACENT ROOM WITH A FREE AREA OF 14,000 MM². THIS EXHAUST SYSTEM MUST BE INTERLOCKED WITH LIGHT SWITCH AND INCLUDE RUN-ON TIMER SO THAT THE EXHAUST SYSTEM CONTINUES TO OPERATE FOR 10 MINUTES AFTER THE LIGHT SWITCH IS OFF.
- ANY INSTALLED - KITCHEN RANGEHOOD EXHAUST TO DISCHARGE DIRECTLY OR VIA DUCT TO OUTDOOR AIR WITH MINIMUM FLOW RATE OF 40L/S & MAKE-UP AIR VIA OPENINGS TO AN ADJACENT ROOM WITH A FREE AREA OF 14,000 MM².
- LAUNDRY EXHAUST TO DISCHARGE DIRECTLY OR VIA DUCT TO OUTDOOR AIR WITH MINIMUM FLOW RATE OF 40L/S & MAKE-UP AIR VIA OPENINGS TO AN ADJACENT ROOM WITH A FREE AREA OF 14,000 MM².



REV	DATE	CC ISSUE	DESCRIPTION	BY
1	11-06-2026	CC ISSUE		



THIS DRAWING IS THE EXCLUSIVE PROPERTY OF THE DEVELOPER & THE REPRODUCTION OF ANY PART WITHOUT THE PRIOR WRITTEN CONSENT OF THE DEVELOPER IS A VIOLATION OF APPLICABLE LAWS. IN NO EVENT SHALL THE DEVELOPER BE HELD LIABLE FOR SPECIAL, COLLATERAL, INCIDENTAL OR CONSEQUENTIAL LIABILITY IN CONNECTION WITH THE USE OF THIS DIGITAL DATA ONCE RELEASED FROM THE DEVELOPERS OFFICE. THIS DRAWING IS TO BE READ & UNDERSTOOD IN CONJUNCTION WITH THE STRUCTURAL, MECHANICAL, ELECTRICAL &/OR ANY OTHER CONSULTANT'S DOCUMENTATION AS MAY BE APPLICABLE TO THE PROJECT PRIOR TO THE START OF ANY WORKS AND FOR ITS DURATION.

PROJECT:
4 TRAVELLERS WAY
LOT 25 IN DP 1289262
No.04 TRAVELLERS WAYS
TAHMOOR NSW

DRAWING TITLE:
GENERAL NOTES

NORTH:

LOT NO:	DATE:	SCALE:	DRAWING No:	REV:
25	1-07-2026	1 : 2	CC.02A	1
DRAWN BY:	CHECKED BY:			ISSUED BY:
ROHIT	RH	Sudip Shreshta and Sanu Laxmi shreshta		
CLIENT NAME:				

TERMITE SHEET

- TERMITE SHEET EXTENDS THROUGH THE ENTIRE MASONRY LEAF AND IS VISIBLE AT THE FINISHED FACE OF THE WALL.


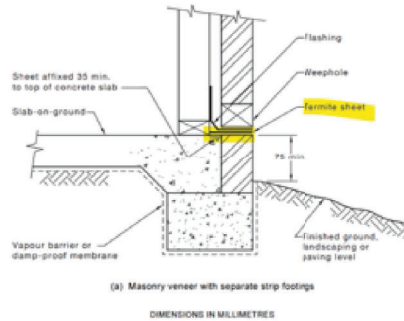


FIGURE 5.5 (in part) TYPICAL SHEET INSTALLATION TO EXTERNAL WALL WITH CONCRETE FLOOR SLAB

DPC FOR BRICKS

DAMP-PROOF COURSE (DPC) TO EXTENDS THROUGH THE ENTIRE MASONRY LEAF AND NEED TO BE VISIBLE AT THE FINISHED FACE OF THE WALL FROM OUTSIDE

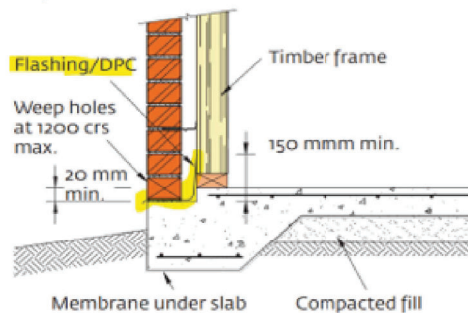

DEMOLITION

- AS 2601-2001 – DEMOLITION WORK

PLANTER BOX

REFER BELOW DETAILS FOR PLANTER BOX.



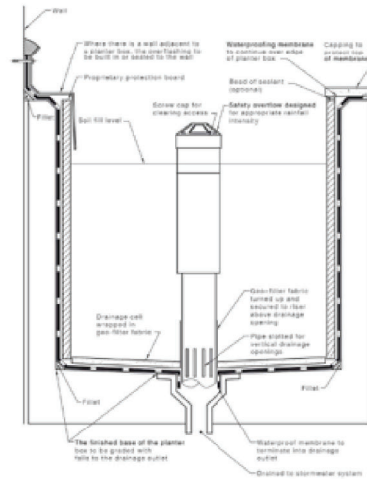


FIGURE 2.17 TYPICAL PLANTER BOX CONSTRUCTION

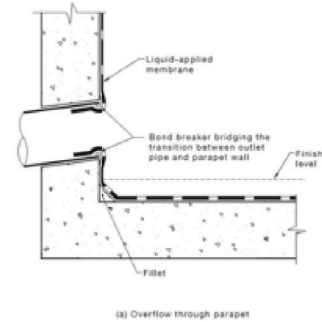

OVERFLOW TO BALCONY:

- SURFACE DRAIN & OVERFLOW TO BALCONY

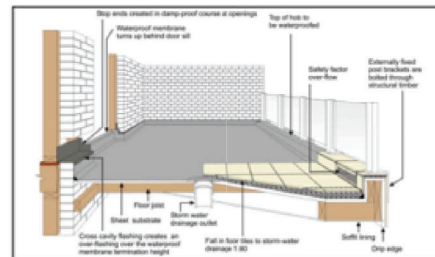

SWIMMING POOL

- PART 12.1.1 (H7D2) OF THE NCC VOLUME 2, AMENDMENT 1 - BUILDING CODE OF AUSTRALIA 2022 & HOUSING PROVISIONS STANDARD 2022
- AS 1926 PART 1-2012 – SWIMMING POOLSAFETY- SAFETY BARRIERS FOR SWIMMING POOLS
- AS 1926 PART 2-2007 - SWIMMING POOL SAFETY- LOCATION OF SAFETY BARRIERS FOR SWIMMING POOLS (INCORPORATING AMENDMENTS 1 AND 2)
- AS 1926 PART 3-2010 – SWIMMING POOL SAFETY- WATER RECIRCULATION SYSTEMS (INCORPORATING AMENDMENT 1)

OnBuild Certifiers Pty Ltd

Reference: 260036

Date: 27/07/2026

Andrew Soliman

Director/ Principal Certifier

BDC2940

Consultant who prepared this document remains responsible for accuracy

REV	DATE	DESCRIPTION	BY



THIS DRAWING IS THE EXCLUSIVE PROPERTY OF THE DEVELOPER & THE REPRODUCTION OF ANY PART WITHOUT THE PRIOR WRITTEN CONSENT OF THE DEVELOPER IS A VIOLATION OF APPLICABLE LAWS. IN NO EVENT SHALL THE DEVELOPER BE HELD LIABLE FOR SPECIAL COLLATERAL, INCIDENTAL OR CONSEQUENTIAL LIABILITY IN CONNECTION WITH THE USE OF THIS DIGITAL DATA ONCE RELEASED FROM THE DEVELOPERS OFFICE. THIS DRAWING IS TO BE READ & UNDERSTOOD IN CONJUNCTION WITH THE STRUCTURAL, MECHANICAL, ELECTRICAL & / OR ANY OTHER CONSULTANT'S DOCUMENTATION AS MAY BE APPLICABLE TO THE PROJECT PRIOR TO THE START OF ANY WORKS AND FOR ITS DURATION.

PROJECT:

4 TRAVELLERS WAY

LOT 25 IN DP 1289262

No.04 TRAVELLERS WAYS

TAHMOOR nsw

DRAWING TITLE:

GENERAL NOTES

NORTH:

LOT NO:

25

DATE:

1-07-2026

SCALE:

1 : 2

DRAWING No:

CC.02B

REV:


ISSUED BY:

CLIENT NAME:

Sudip Shreshta and Sanu Laxmi shreshta

CC ISSUE

Subject to
condition
21 of the
consent

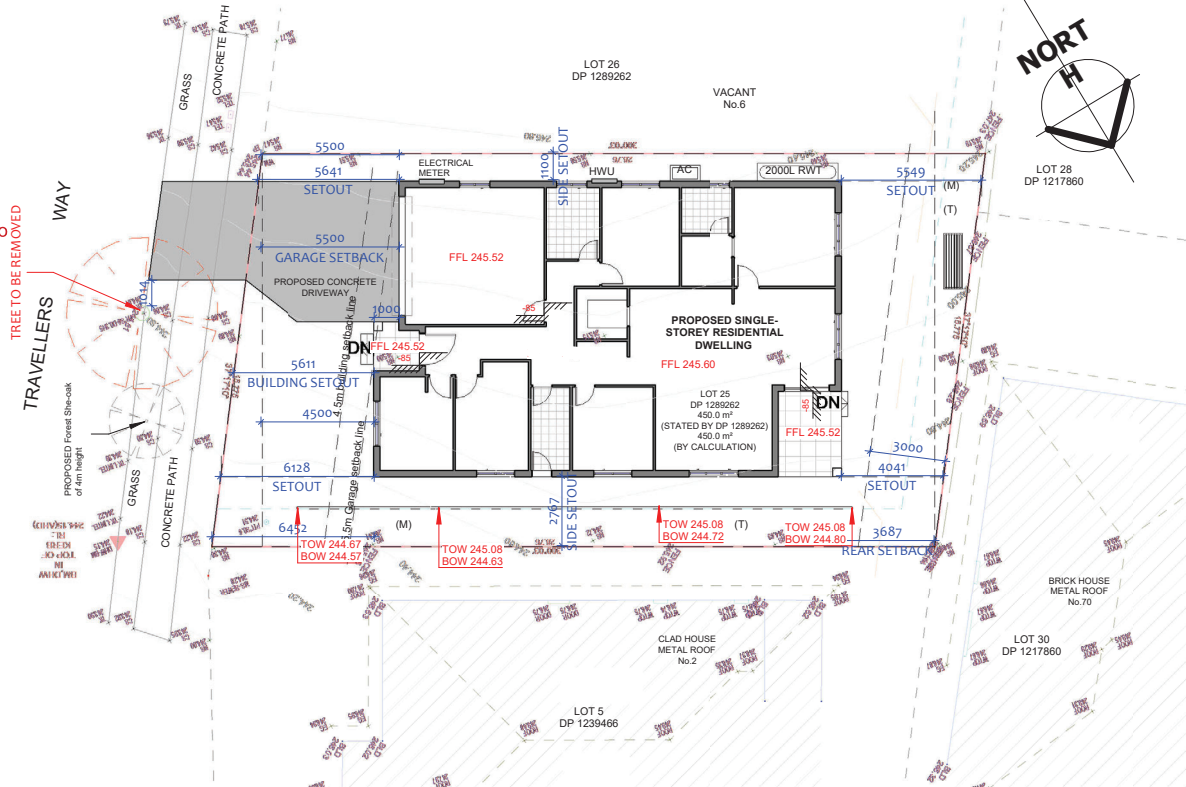

CC - SITE PLAN

1 : 200

(M) - EASEMENT TO DRAIN WATER 1.5 WIDE (DP 1274639) (NO.1) (VIDE DP 1289262)
(T) - EASEMENT TO DRAIN WATER 1.5 WIDE (NO.1) (VIDE DP 1289262)

OnBuild Certifiers Pty Ltd
Reference: 260036
Date: 27/07/2026
Andrew Soliman
Director/ Principal Certifier
BDC2940

CODE COMPLIANCE TABLE				
Wollondilly Development Control Plan 2016 Volume 6 - Residential Development				
DESCRIPTION	REQUIREMENT	PROPOSED	COMPLIANCE	
ELEMENT	CODE CONTROL	REQUIREMENT	PROPOSED	COMMENT
LAND ZONE	R2 - Low Density Residential			
LOT NO	LOT 25			
LOT AREA	450.0 m2			
LOT WIDTH	Standard Lot Min. 6m at Building Line facing primary road	6.0m	14.85 m	YES
HEIGHT	MAX. Height	8.5m	5m (MAX.)	YES
FRONT SETBACK	FRONT SET BACK (Min. Setback from Primary Road)	4.5 m	5.6m	YES
REAR SETBACK (MIN.)	GROUND FLOOR	3m	4.04m	YES
	FIRST FLOOR	8m	NA	YES
SIDE SETBACK (MIN.)	GROUND FLOOR	0.9/0.9m	1.1/2.7m	YES
	FIRST FLOOR	0.9/0.9m	NA	YES
COVERAGE AREA	The total portion of the site covered by buildings shall not exceed 60% of the site area.	270SQM(60%)	202SQM(45%)	YES
PRIVATE OPEN SPACE		16m2	24 m2	YES
LANDSCAPE AREA			175.0 m2	

CC ISSUE

REV	DATE	DESCRIPTION	BY
1	11-06-2026	CC ISSUE	


RUBY HOMES

THIS DRAWING IS THE EXCLUSIVE PROPERTY OF THE DEVELOPER & THE REPRODUCTION OF ANY PART WITHOUT THE PRIOR WRITTEN CONSENT OF THE DEVELOPER IS A VIOLATION OF APPLICABLE LAWS. IN NO EVENT SHALL THE DEVELOPER BE HELD LIABLE FOR SPECIAL, COLLATERAL, INCIDENTAL OR CONSEQUENTIAL LIABILITY IN CONNECTION WITH THE USE OF THIS DIGITAL DATA ONCE RELEASED FROM THE DEVELOPER'S OFFICE. THIS DRAWING IS TO BE READ & UNDERSTOOD IN CONJUNCTION WITH THE STRUCTURAL, MECHANICAL, ELECTRICAL &/OR ANY OTHER CONSULTANT'S DOCUMENTATION AS MAY BE APPLICABLE TO THE PROJECT PRIOR TO THE START OF ANY WORKS AND FOR ITS DURATION.

PROJECT:
4 TRAVELLERS WAY
LOT 25 IN DP 1289262
No.04 TRAVELLERS WAYS
TAHMOOR nsw

DRAWING TITLE:
**LOCATION PLAN
AND SITE PLAN**



LOT NO:	25	DATE:	1-07-2026	SCALE:	As indicated	DRAWING No:	CC.03	REV:	1
DRAWN BY:	ROHIT	CHECKED BY:	RH					ISSUED BY:	
CLIENT NAME: Sudip Shreshta and Sanu Laxmi shreshta									

OnBuild Construction Ltd
Reference: 2026/00000000
Date: 11-06-2026
Andrew Scrimshaw
Director/ Principal Designer
BACS 3540
Consultant who prepared this document
remains responsible for accuracy

IMPORTANT NOTES:
ALL DIMENSIONS AND NOTES ON ALL PLANS MUST BE CHECKED AND VERIFIED BY BUILDERS AND OWNER PRIOR TO COMMENCEMENT OF ANY BUILDING WORKS. TO CLARIFY AND CONFIRM WITH CONSTRUCTION COMPANY FOR DISCREPANCIES ON ALL DOCUMENTS AND PLANS PROVIDED FOR CONSTRUCTION. ANY WORK INDICATED ON THE PLAN BUT NOT IN CONTRACT, VARIATION TO PLANS, SPECIFICATIONS MAY NOT BE THE RESPONSIBILITY OF THE BUILDING USER TO VERIFY PLANS CURRENT BCA AND AUSTRALIAN STANDARDS. WINDOWS TO COMPLY WITH 3.9.3.5 OF THE BCA.



1- CC - CUT AND FILL
1 : 200

NOTE: PLEASE REFER TO TENDER FOR ALL INCLUSIONS.

REV	DATE	DESCRIPTION	BY
1	11-06-2026	CC ISSUE	



RUBY HOMES

THIS DRAWING IS THE EXCLUSIVE PROPERTY OF THE DEVELOPER & THE REPRODUCTION OF ANY PART WITHOUT THE PRIOR WRITTEN CONSENT OF THE DEVELOPER IS A VIOLATION OF APPLICABLE LAWS. IN NO EVENT SHALL THE DEVELOPER BE HELD LIABLE FOR SPECIAL, COLLATERAL, INCIDENTAL OR CONSEQUENTIAL LIABILITY IN CONNECTION WITH THE USE OF THIS DIGITAL DATA ONCE RELEASED FROM THE DEVELOPER'S OFFICE. THIS DRAWING IS TO BE READ & UNDERSTOOD IN CONJUNCTION WITH THE STRUCTURAL, MECHANICAL, ELECTRICAL &/OR ANY OTHER CONSULTANT'S DOCUMENTATION AS MAY BE APPLICABLE TO THE PROJECT PRIOR TO THE START OF ANY WORKS AND FOR ITS DURATION.


PROJECT:
4 TRAVELLERS WAY
LOT 25 IN DP 1289262
No.04 TRAVELLERS WAYS
TAHMOOR nsw

DRAWING TITLE:
**CUT AND FILL
PLAN**

NORTH:



LOT NO:	DATE:	SCALE:	DRAWING No:	REV:
25	1-07-2026	1 : 200	CC.04	1
DRAWN BY:	CHECKED BY:			ISSUED BY:
ROHIT	RH			
CLIENT NAME: Sudip Shreshta and Sanu Laxmi shreshta				

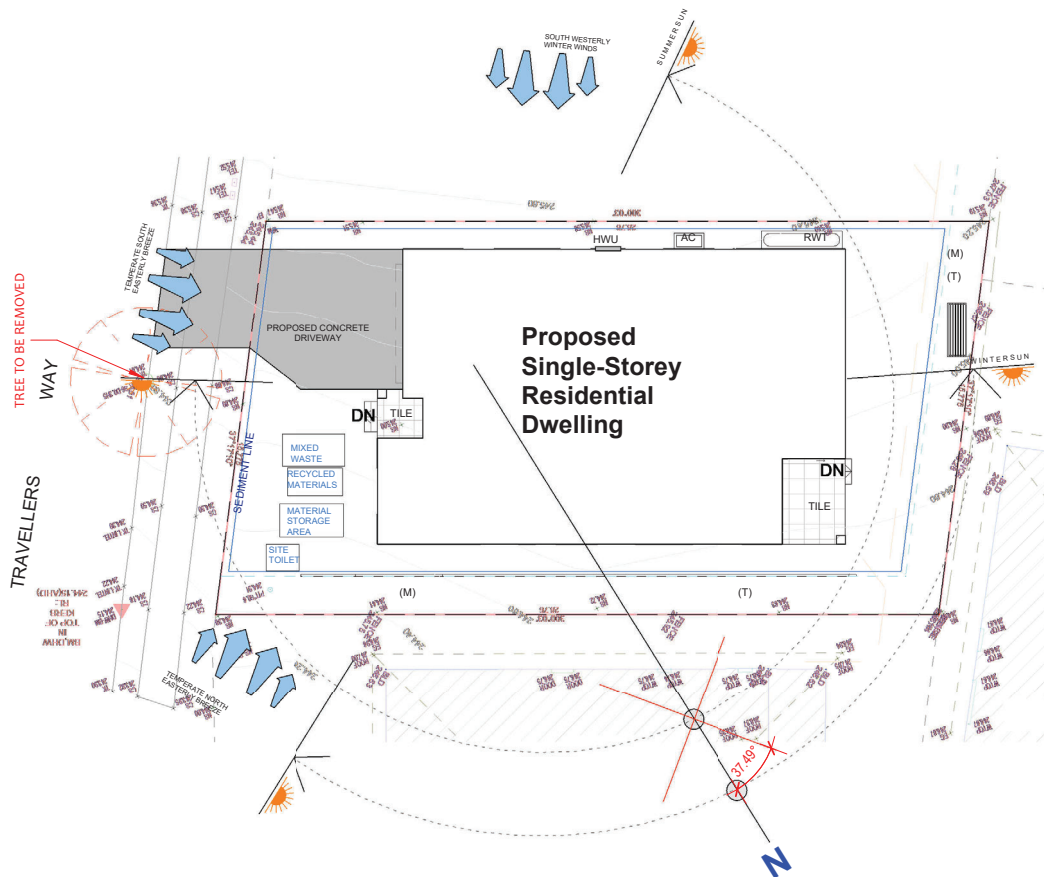

CC - SITE ANALYSIS AND SEDIMENT CONTROL

1 : 200

SD 5-7 STABILISED SITE ACCESS

- 1) STRIP TOPSOIL AND LEVEL SITE.
- 2) COMPACT SUBGRADE.
- 3) COVER AREA WITH GEOTEXTILE.
- 4) CONSTRUCT 200 mm THICK PAD OVER GEOTEXTILE USING ROADBASE OR 30 mm AGGREGATE.
- 5) CONSTRUCT HUMP IMMEDIATELY WITHIN BOUNDARY TO DIVERT WATER TO A SEDIMENT FENCE OR OTHER SEDIMENT TRAP.

OnBuild Certificate

Reference: 2

Date: 27/07/2026

Andrew Soliman

Director/Principal Engineer

BPE2940

Consultant who prepares remains responsible




SEDIMENT AND EROSION NOTES:

THIS PLAN IS TO BE READ IN CONJUNCTION WITH SEDIMENT AND EROSION CONTROL DETAILS AS ATTACHED. THE CONTRACTOR SHALL IMPLEMENT ALL SOIL EROSION AND SEDIMENT CONTROL MEASURES AS NECESSARY AND TO THE SATISFACTION OF COUNCIL PRIOR TO THE COMMENCEMENT AND DURING CONSTRUCTION NO DISTURBANCE TO THE SITE SHALL BE PERMITTED OTHER THAN IN THE IMMEDIATE AREA OF THE WORK AND NO MATERIAL SHALL BE REMOVED FROM THE SITE WITHOUT COUNCIL'S APPROVAL. ALL SEDIMENT AND EROSION CONTROL DEVICES TO BE INSTALLED AND MAINTAINED IN ACCORDANCE WITH STANDARDS OUTLINED IN NSW DEPARTMENT OF HOUSING 'MANAGING URBAN STORMWATER: SOLS AND CONSTRUCTIONS'.

TOPSOIL SHALL BE STRIPPED AND STOCKPILED OUTSIDE THE BOUNDARY OF THE SITE. THIS TOPSOIL IS TO BE REVEGETATED LATER ON AREAS TO BE REVEGETATED AND STABILISED ONLY. (IE ALL FOOTPATH BATTERS, SITE BORDERS, GULLIES, DRAINAGE LINES AND CATCH DRAINS). TOPSOIL SHALL NOT BE REVEGETATED ON ANY OTHER AREAS UNLESS SPECIALLY INSTRUCTED BY THE SUPERINTENDENT IF THEY ARE TO REMAIN FOR LONGER THAN ONE MONTH STOCKPILES SHALL BE PROTECTED FROM EROSION BY COVERING THEM WITH A MULCH AND HYDROSEEDING AND IF NECESSARY BY LOCATING BANKS OR DRAINS DOWNSTREAM OF A STOCKPILE TO RETARD SILT LADEN RUNOFF.

THE CONTRACTOR SHALL REGULARLY MAINTAIN ALL SEDIMENT AND EROSION CONTROL DEVICES AND REMOVE ACCUMULATED SILT FROM SUCH DEVICES SUCH THAT MORE THAN 80% OF THEIR CAPACITY LOST. ALL THE SILTS TO BE PLACED OUTSIDE THE LIMIT OF WORKS. THE PERIOD FOR MAINTAINING THESE DEVICES SHALL BE AT LEAST UNTIL ALL DISTURBED AREAS ARE REVEGETATED AND FURTHER AS MAY BE DIRECTED BY THE SUPERINTENDENT OR COUNCIL. LAY TURF STRIP (MIN 300 mm WIDE) ON 100 mm TOPSOIL WITH 10 mm LONG RETURNS EVERY 6.0m BEHIND ALL KERB AT THE TOP OF ALL BATTERS AND AROUND STRUCTURES IMMEDIATELY AFTER BACKFILLING OR FORMATION. THE CONTRACTOR SHALL GRASS SEED ALL DISTURBED AREAS WITH AN APPROVED MIX AS SSON AS PRACTICABLE AFTER COMPLETION OF EARTHWORKS AND REGRADING. VEHICULAR TRAFFIC SHALL BE CONTROLLED DURING CONSTRUCTION CONFINING ACCESS WHERE POSSIBLE TO NOMINATED STABILISED ACCESS POINTS.


WHEN ANY DEVICES ARE TO BE HANDLED OVER TO COUNCIL THEY SHALL BE IN CLEAN AND STABLE CONDITION. THE CONTRACTOR SHALL IMPLEMENT DUST CONTROL BY REGULAR WETTING DOWN BUT NOT SATURATING DISTURBED AREA. PROVIDE AND MAINTAIN SILT TRAPS AROUND ALL SURFACE INLET PITS UNTIL CATCHMENT IS REVEGETATED OR PAVED. REVEGETATE ALL TRENCHES IMMEDIATELY UPON COMPLETION OF BACKFILLING. ALL DRAINAGE PIPE INLETS TO BE CAPPED UNTIL: A) DOWNPIPES CONNECTED B) PITS CONSTRUCTED & PROTECTED WITH SILT BARRIER

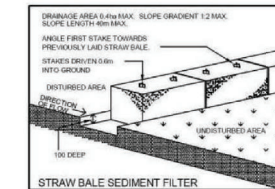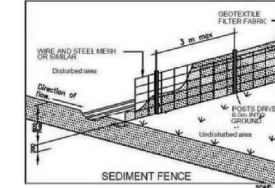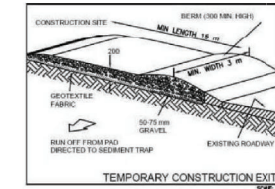

TEMPORARY 1.8M HIGH WIRE MESH FENCE WITH DUSTPROOF MESH APPLIED TO FULL HEIGHT BOUNDARIES AS REQUIRED. LOCATION OF WASTE BINS. SEDIMENT FENCE AS REQUIRED. GRAVEL ACCESS. SITE ACCESS AREA TO BE USED FOR WASHDOWN AREA. FOOTPATH CLEAN AND CLEAR AT ALL TIMES. LOCATION OF STOCKPILE MATERIAL. MATERIAL STORAGE AREA. TEMPORARY TOILETS. INSTALL TEMPORARY SEDIMENT BARRIERS TO ALL INLET PITS LIKELY TO COLLECT SILT LADEN WATER, TO COUNCIL'S REQUIREMENTS.

SD 6-9 GEOTEXTILE INLET FILTER

- 1) FABRICATE A SEDIMENT BARRIER MADE FROM GEOTEXTILE. REFER SD-7 FOR DETAILS.
- 2) SUPPORT GEOTEXTILE WITH MESH TIED TO POSTS AT 1 m CTRS.
- 3) DO NOT COVER INLET WITH GEOTEXTILE.

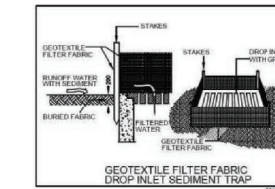

SITE WORKS NOTES

1. ORIGIN OF LEVELS PROVIDED BY SURVEYOR
2. THE BUILDER SHALL VERIFY ALL DIMENSIONS AND EXISTING LEVELS ON SITE PRIOR TO THE COMMENCEMENT OF WORK AND ANY DISCREPANCIES SHALL BE REPORTED TO THE SURVEYOR/ENGINEER.
3. TOPSOIL SHALL BE STRIPPED FROM THE CONSTRUCTION AREA AND STOCKPILED ON SITE. TO BE LATER SPREAD OR DISPOSED OFF SITE, AS DIRECTED BY SUPERVISOR/ENGINEER.
4. ALL TRENCH BACKFILL MATERIAL SHALL BE COMPACTED TO THE SAME DENSITY AS THE ADJACENT MATERIAL.
5. ALL SERVICE TRENCHES UNDER VEHICULAR PAVEMENTS SHALL BE BACKFILLED WITH SAND OR APPROVED GRANULAR MATERIALS. TO THE UNDERSIDE OF THE PAVEMENT, AND COMPACTED TO 98% STANDARD MAXIMUM DRY DENSITY, IN ACCORDANCE WITH AS 12898.1.1.

CC ISSUE


REV	DATE	DESCRIPTION	BY
1	11-06-2026	CC ISSUE	

RUBY HOMES

THIS DRAWING IS THE EXCLUSIVE PROPERTY OF THE DEVELOPER & THE REPRODUCTION OF ANY PART WITHOUT THE PRIOR WRITTEN CONSENT OF THE DEVELOPER IS A VIOLATION OF APPLICABLE LAWS. IN NO EVENT SHALL THE DEVELOPER BE HELD LIABLE FOR SPECIAL, COLLATERAL, INCIDENTAL OR CONSEQUENTIAL LIABILITY IN CONNECTION WITH THE USE OF THIS DIGITAL DATA ONCE RELEASED FROM THE DEVELOPER'S OFFICE. THIS DRAWING IS TO BE READ & UNDERSTOOD IN CONJUNCTION WITH THE STRUCTURAL, MECHANICAL, ELECTRICAL &/OR ANY OTHER CONSULTANT'S DOCUMENTATION AS MAY BE APPLICABLE TO THE PROJECT PRIOR TO THE START OF ANY WORKS AND FOR ITS DURATION.

PROJECT:
4 TRAVELLERS WAY
LOT 25 IN DP 1289262
No.04 TRAVELLERS WAYS
TAHMOOR NSW


DRAWING TITLE:
SITE ANALYSIS AND SEDIMENT CONTROL

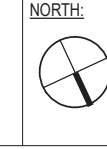

LOT NO:	DATE:	SCALE:	DRAWING No:	REV:
25	1-07-2026	As indicated	CC.05	1
DRAWN BY:	CHECKED BY:	CLIENT NAME:	ISSUED BY:	
ROHIT	RH	Sudip Shreshta and Sanu Laxmi shreshta		

OnBuild Construction Ltd
Reference: 25/2026
Date: 1-07-2026
Andrew Schuman
Director/ Principal Designer
BACS TEAM
Consultant who prepared this document remains responsible for accuracy

IMPORTANT NOTES:
ALL DIMENSIONS AND NOTES ON ALL PLANS MUST BE CHECKED AND VERIFIED BY BUILDERS AND OWNER PRIOR TO COMMENCEMENT OF ANY BUILDING WORKS. TO CLARIFY AND CONFIRM WITH CONSTRUCTION COMPANY FOR DISCREPANCIES ON ALL DOCUMENTS AND PLANS PROVIDED FOR CONSTRUCTION. ANY WORK INDICATED ON THE PLAN BUT NOT IN CONTRACT, VARIATION TO PLANS. SPECIFICATIONS MAY NOT BE THE RESPONSIBILITY OF THE BUILDER. END USER TO VERIFY PLANS CURRENT BCA AND AUSTRALIAN STANDARDS. WINDOWS TO COMPLY WITH 3.9.3.5 OF THE BCA.

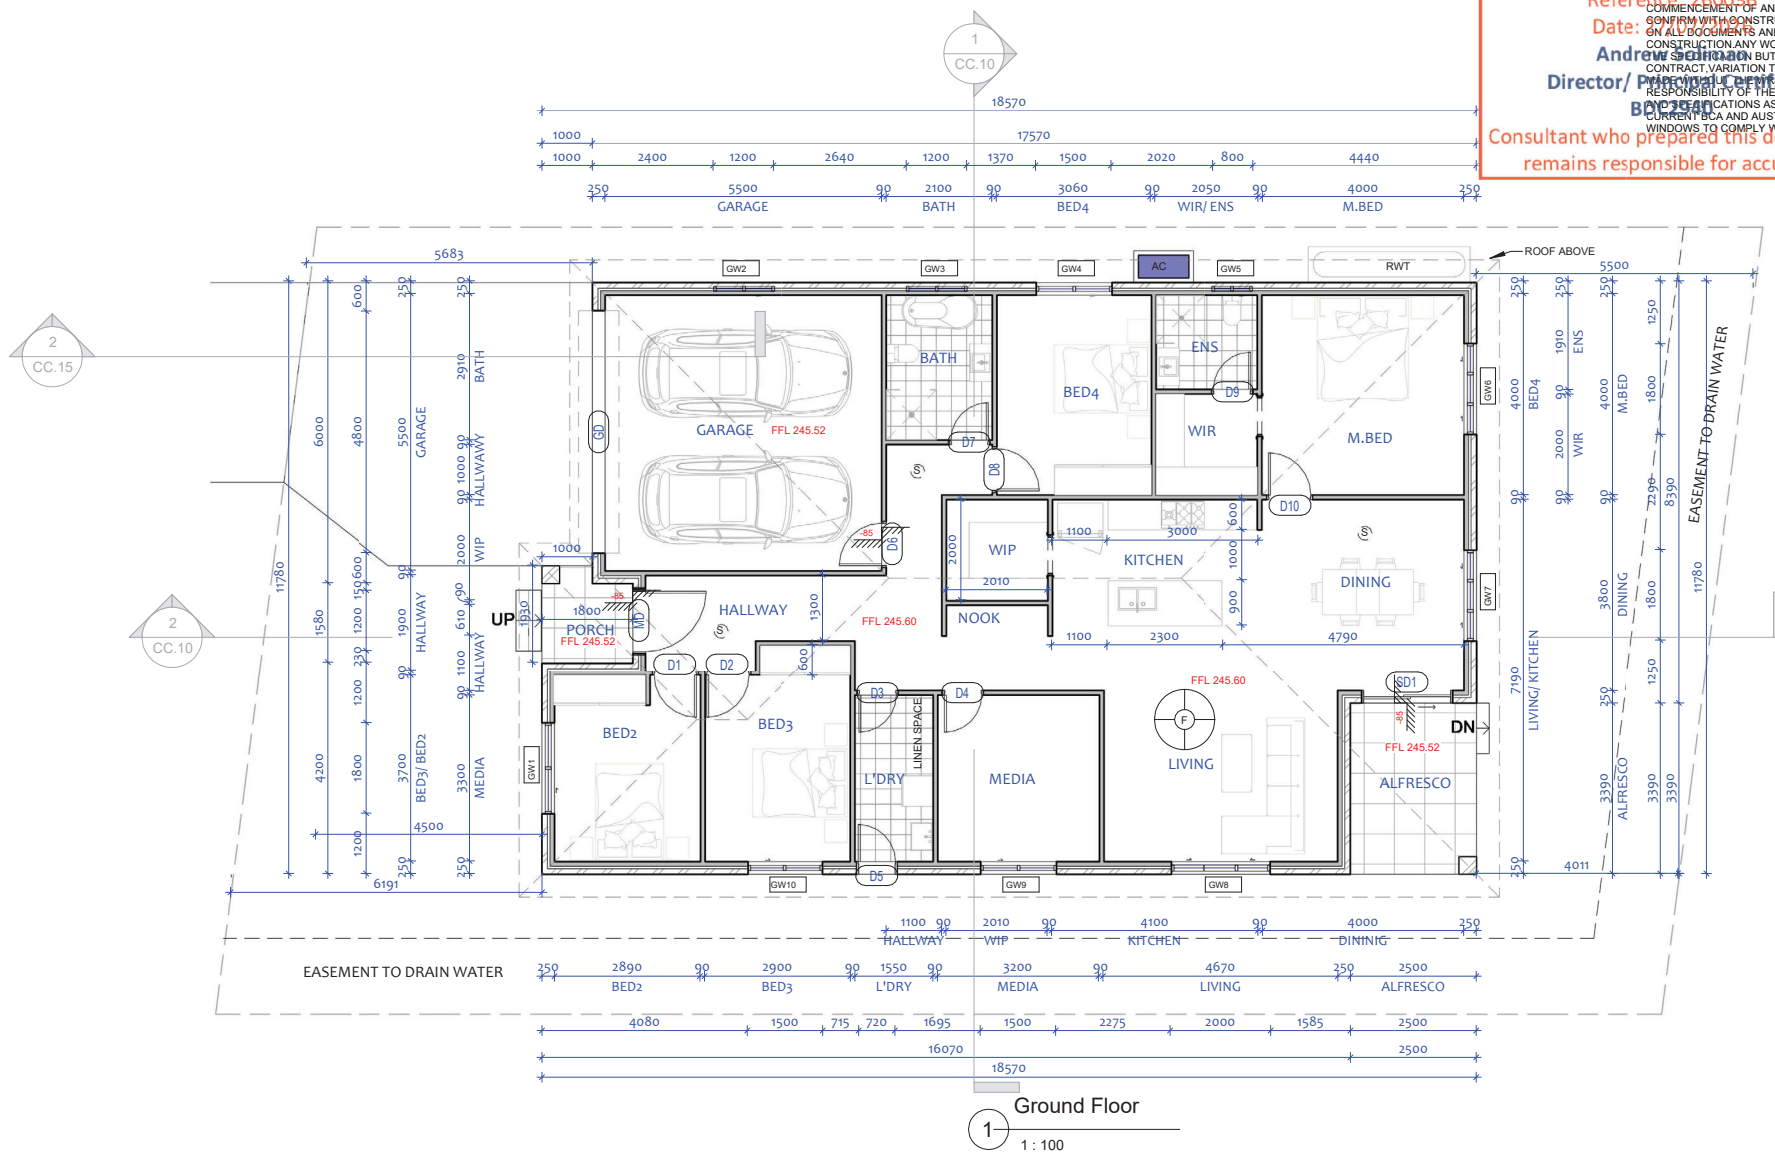

NOTE: PLEASE REFER TO TENDER FOR ALL INCLUSIONS.

REV	DATE	DESCRIPTION	BY
1	11-06-2026	CC ISSUE	



RUBY HOMES


THIS DRAWING IS THE EXCLUSIVE PROPERTY OF THE DEVELOPER & THE REPRODUCTION OF ANY PART WITHOUT THE PRIOR WRITTEN CONSENT OF THE DEVELOPER IS A VIOLATION OF APPLICABLE LAWS. IN NO EVENT SHALL THE DEVELOPER BE HELD LIABLE FOR SPECIAL, COLLATERAL, INCIDENTAL OR CONSEQUENTIAL LIABILITY IN CONNECTION WITH THE USE OF THIS DIGITAL DATA ONCE RELEASED FROM THE DEVELOPERS OFFICE. THIS DRAWING IS TO BE READ & UNDERSTOOD IN CONJUNCTION WITH THE STRUCTURAL, MECHANICAL, ELECTRICAL & / OR ANY OTHER CONSULTANT DOCUMENTATION AS MAY BE APPLICABLE TO THE PROJECT PRIOR TO THE START OF ANY WORKS AND FOR ITS DURATION.

PROJECT:
4 TRAVELLERS WAY
LOT 25 IN DP 1289262
No.04 TRAVELLERS WAYS
TAHMOOR nsw

DRAWING TITLE:
GROUND FLOOR PLAN



				CC ISSUE	
LOT NO:	DATE:	SCALE:	DRAWING No:	REV:	1
25	1-07-2026	1 : 100	CC.06	ISSUED BY:	
DRAWN BY:	CHECKED BY:				
ROHIT	RH				
CLIENT NAME:					
Sudip Shreshta and Sanu Laxmi shreshta					

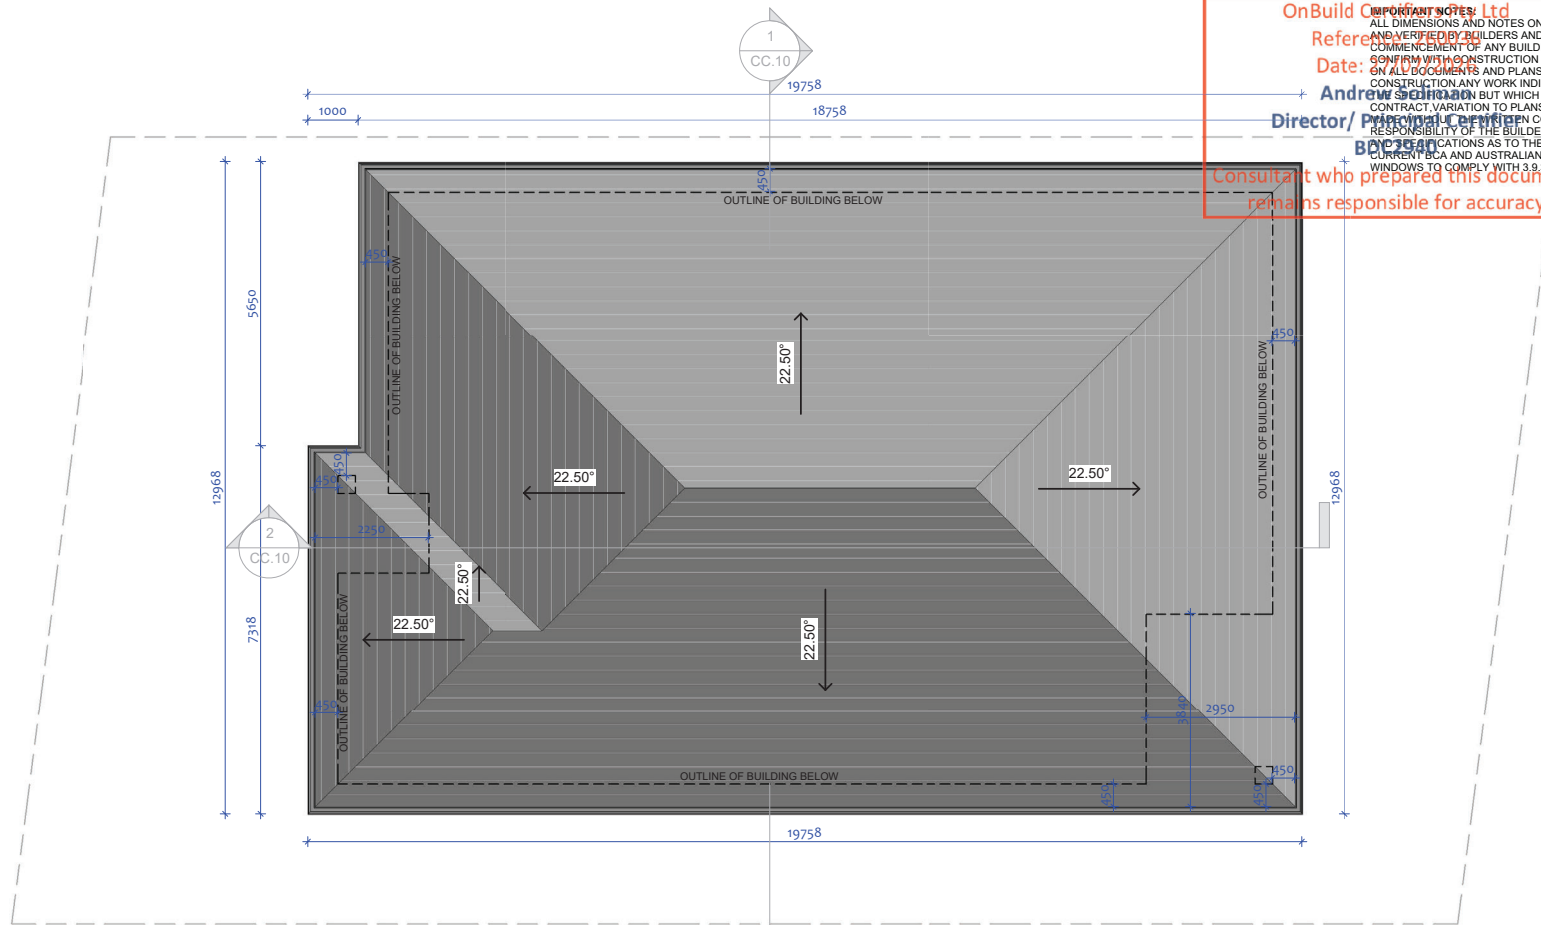

1 ROOF PLAN
1 : 100

Roof Schedule			
Mark	Base Level	Area	Comments
R1	Ground Ceiling	261 m ²	TILE ROOF

REV	DATE	DESCRIPTION	BY
1	11-06-2026	CC ISSUE	




RUBY HOMES

THIS DRAWING IS THE EXCLUSIVE PROPERTY OF THE DEVELOPER & THE REPRODUCTION OF ANY PART WITHOUT THE PRIOR WRITTEN CONSENT OF THE DEVELOPER IS A VIOLATION OF APPLICABLE LAWS. IN NO EVENT SHALL THE DEVELOPER BE HELD LIABLE FOR SPECIAL, COLLATERAL, INCIDENTAL OR CONSEQUENTIAL LIABILITY IN CONNECTION WITH THE USE OF THIS DIGITAL DATA ONCE RELEASED FROM THE DEVELOPER'S OFFICE. THIS DRAWING IS TO BE READ & UNDERSTOOD IN CONJUNCTION WITH THE STRUCTURAL, MECHANICAL, ELECTRICAL & / OR ANY OTHER CONSULTANT'S DOCUMENTATION AS MAY BE APPLICABLE TO THE PROJECT PRIOR TO THE START OF ANY WORKS AND FOR ITS DURATION.

PROJECT:
4 TRAVELLERS WAY
LOT 25 IN DP 1289262
No.04 TRAVELLERS WAYS
TAHMOOR nsw

DRAWING TITLE:
ROOF PLAN

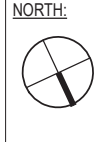

LOT NO:	DATE:	SCALE:	DRAWING No:	REV:
25	1-07-2026	1 : 100	CC.07	1
DRAWN BY:	CHECKED BY:	ISSUED BY:		
ROHIT	RH	Sudip Shreshta and Sanu Laxmi shreshta		

OnBuild Certifiers Pty Ltd
Reference: 260036
Date: 27/07/2026
Andrew Soliman
Director/ Principal Certifier

BDC2940

Window Schedule
Consultant who prepared this document

Mark	Height	Width	Height	Head Height	Description
------	--------	-------	--------	-------------	-------------

Ground Floor

GW1	1850	1800	550	2400	SLIDING
GW2	800	1200	1600	2400	SLIDING
GW3	800	1200	1600	2400	SLIDING
GW4	1400	1500	1000	2400	SLIDING
GW5	800	800	1600	2400	SLIDING
GW6	1850	1800	550	2400	SLIDING & FIXED
GW7	1400	1800	1000	2400	SLIDING & FIXED
GW8	1400	2000	1000	2400	SLIDING & FIXED
GW9	1400	1500	1000	2400	SLIDING
GW10	1400	1500	1000	2400	SLIDING

Ground Floor: 10



Door Schedule 1

Mark	Height	Width	Count	Description
------	--------	-------	-------	-------------

Ground Floor

D1	2340	820	1	FLUSH DOOR
D2	2340	820	1	FLUSH DOOR
D3	2340	720	1	FLUSH DOOR
D4	2340	720	1	FLUSH DOOR
D5	2340	720	1	FLUSH DOOR
D6	2340	820	1	FLUSH DOOR
D7	2340	720	1	FLUSH DOOR
D8	2340	820	1	FLUSH DOOR
D9	2340	720	1	FLUSH DOOR
D10	2340	820	1	FLUSH DOOR
GD	2400	4800	1	GARAGE DOOR
MD	2400	1200	1	SOLID CORE DOOR
SD1	2300	1800	1	SLIDING DOOR

Ground Floor: 13

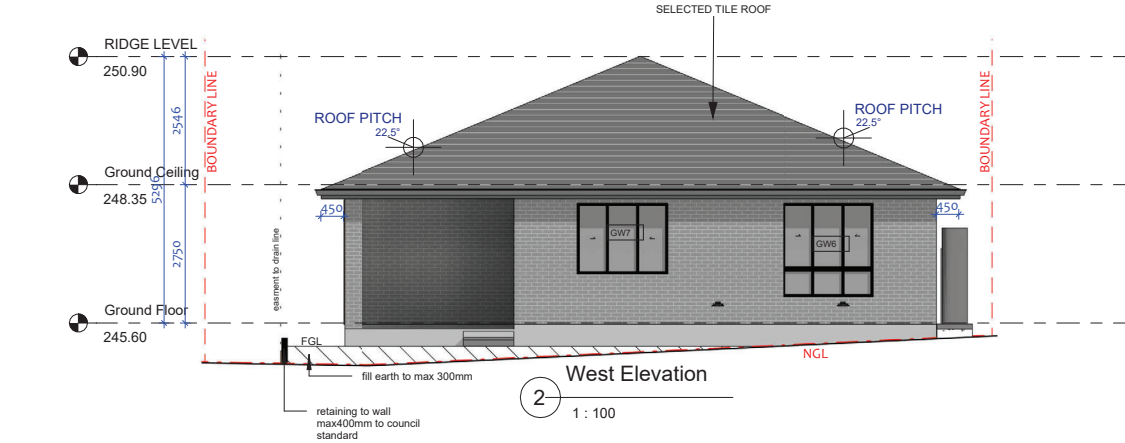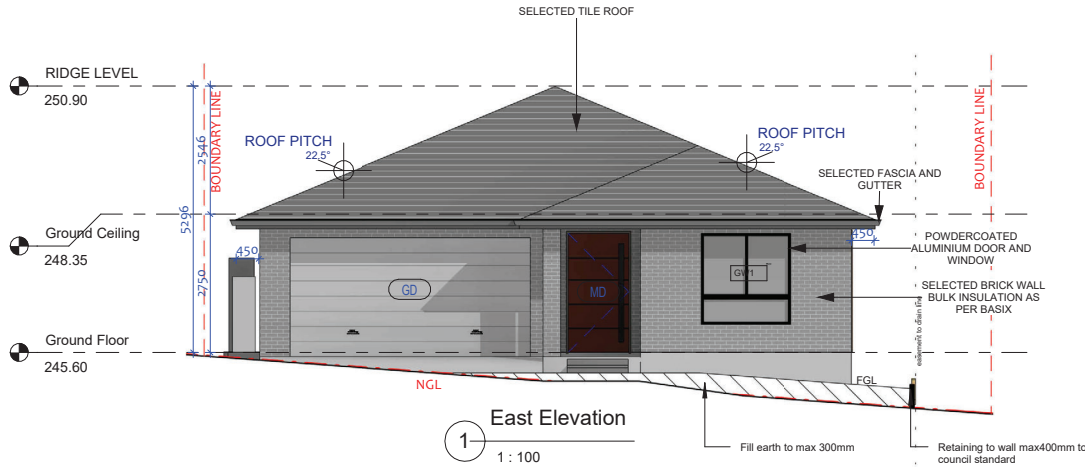

REV	DATE	DESCRIPTION	BY
1	11-06-2026	CC ISSUE	




PROJECT:
4 TRAVELLERS WAY
LOT 25 IN DP 1289262
No.04 TRAVELLERS WAYS
TAHMOOR nsw

DRAWING TITLE:
ELEVATION 01

NORTH:

LOT NO:	DATE:	SCALE:	DRAWING No:	REV:
25	1-07-2026	1 : 100	CC.08	1
DRAWN BY:	CHECKED BY:			ISSUED BY:
ROHIT	RH			
CLIENT NAME: Sudip Shreshta and Sanu Laxmi shreshta				

OnBuild Certifiers Pty Ltd
Reference: 260036
Date: 27/07/2026
Andrew Soliman
Director/ Principal Certifier
BDC2940
Consultant who prepared this document
remains responsible for accuracy

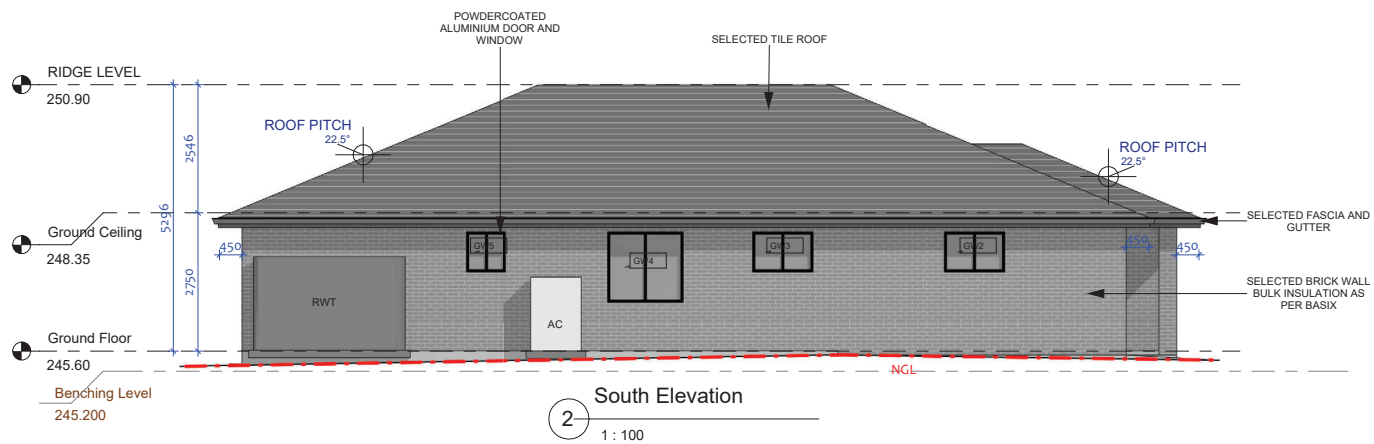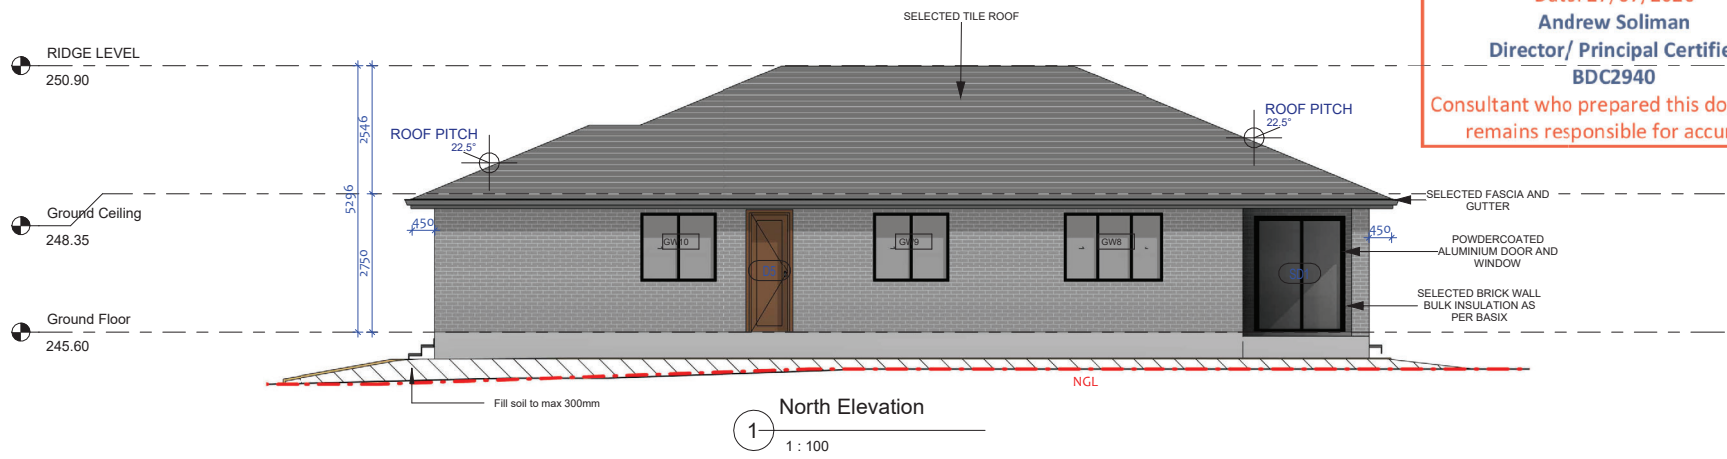

REV	DATE	DESCRIPTION	BY
1	11-06-2026	CC ISSUE	


RUBY HOMES

THIS DRAWING IS THE EXCLUSIVE PROPERTY OF THE DEVELOPER & THE REPRODUCTION OF ANY PART WITHOUT THE PRIOR WRITTEN CONSENT OF THE DEVELOPER IS A VIOLATION OF APPLICABLE LAWS. IN NO EVENT SHALL THE DEVELOPER BE HELD LIABLE FOR SPECIAL COLLATERAL, INCIDENTAL OR CONSEQUENTIAL LIABILITY IN CONNECTION WITH THE USE OF THIS DIGITAL DATA ONCE RELEASED FROM THE DEVELOPERS OFFICE. THIS DRAWING IS TO BE READ & UNDERSTOOD IN CONJUNCTION WITH THE STRUCTURAL, MECHANICAL, ELECTRICAL & / OR ANY OTHER CONSULTANTS DOCUMENTATION AS MAY BE APPLICABLE TO THE PROJECT PRIOR TO THE START OF ANY WORKS AND FOR ITS DURATION.


PROJECT:
4 TRAVELLERS WAY
LOT 25 IN DP 1289262
No.04 TRAVELLERS WAYS
TAHMOOR nsw

DRAWING TITLE:
ELEVATION 02


NORTH:

LOT NO:	DATE:	SCALE:	DRAWING No:	REV:
25	1-07-2026	1 : 100	CC.09	1
DRAWN BY:	CHECKED BY:	CLIENT NAME:	ISSUED BY:	
ROHIT	RH	Sudip Shreshta and Sanu Laxmi shreshta		

OnBuild Certifiers Pty Ltd
Reference: 260036
Date: 27/07/2026
Andrew Soliman
Director/ Principal Certifier
BDC2940
Consultant who prepared this document
remains responsible for accuracy

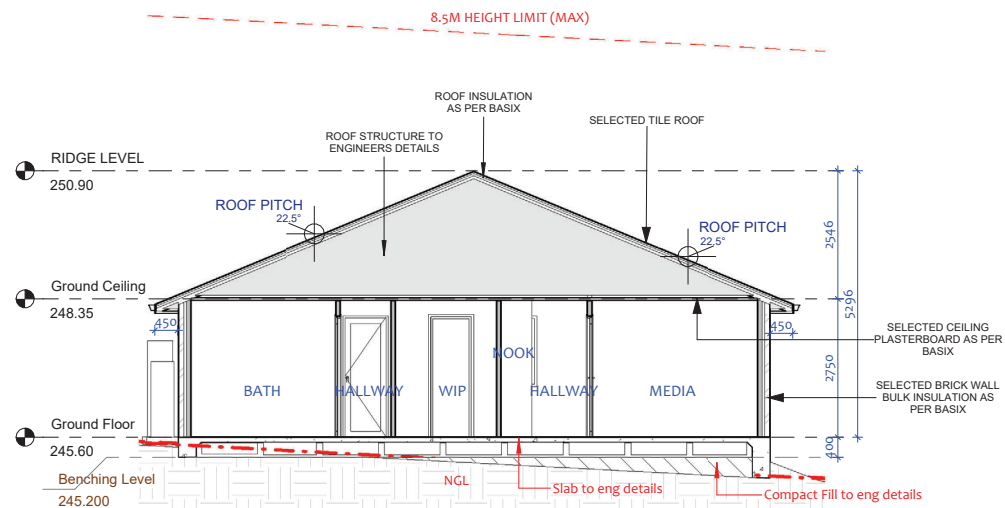

1 CROSS SECTION
1 : 100

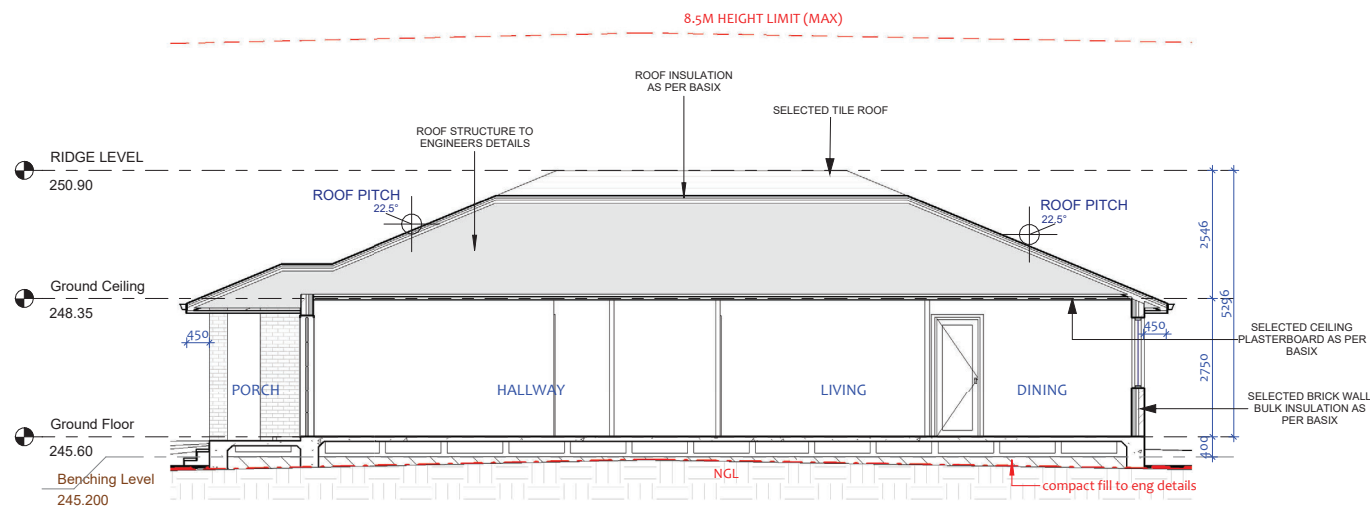

2 LONGITUDINAL SECTION
1 : 100

REV	DATE	DESCRIPTION	BY
1	11-06-2026	CC ISSUE	


RUBY HOMES

THIS DRAWING IS THE EXCLUSIVE PROPERTY OF THE DEVELOPER & THE REPRODUCTION OF ANY PART WITHOUT THE PRIOR WRITTEN CONSENT OF THE DEVELOPER IS A VIOLATION OF APPLICABLE LAWS. IN NO EVENT SHALL THE DEVELOPER BE HELD LIABLE FOR SPECIAL, COLLATERAL, INCIDENTAL OR CONSEQUENTIAL LIABILITY IN CONNECTION WITH THE USE OF THIS DIGITAL DATA ONCE RELEASED FROM THE DEVELOPER'S OFFICE. THIS DRAWING IS TO BE READ & UNDERSTOOD IN CONJUNCTION WITH THE STRUCTURAL, MECHANICAL, ELECTRICAL &/OR ANY OTHER CONSULTANT'S DOCUMENTATION AS MAY BE APPLICABLE TO THE PROJECT PRIOR TO THE START OF ANY WORKS AND FOR ITS DURATION.

PROJECT:
4 TRAVELLERS WAY
LOT 25 IN DP 1289262
No.04 TRAVELLERS WAYS
TAHMOOR nsw


DRAWING TITLE:
SECTIONS

NORTH:

LOT NO:	DATE:	SCALE:	DRAWING No:	REV:
25	1-07-2026	1 : 100	CC.10	1
DRAWN BY:	CHECKED BY:			ISSUED BY:
ROHIT	RH			
CLIENT NAME: Sudip Shreshta and Sanu Laxmi shreshta				

CC ISSUE

OnBuild Certifiers Pty Ltd
Reference: 260036
Date: 27/07/2026
Andrew Soliman
Director/ Principal Certifier
BDC2940
Consultant who prepared this document
remains responsible for accuracy

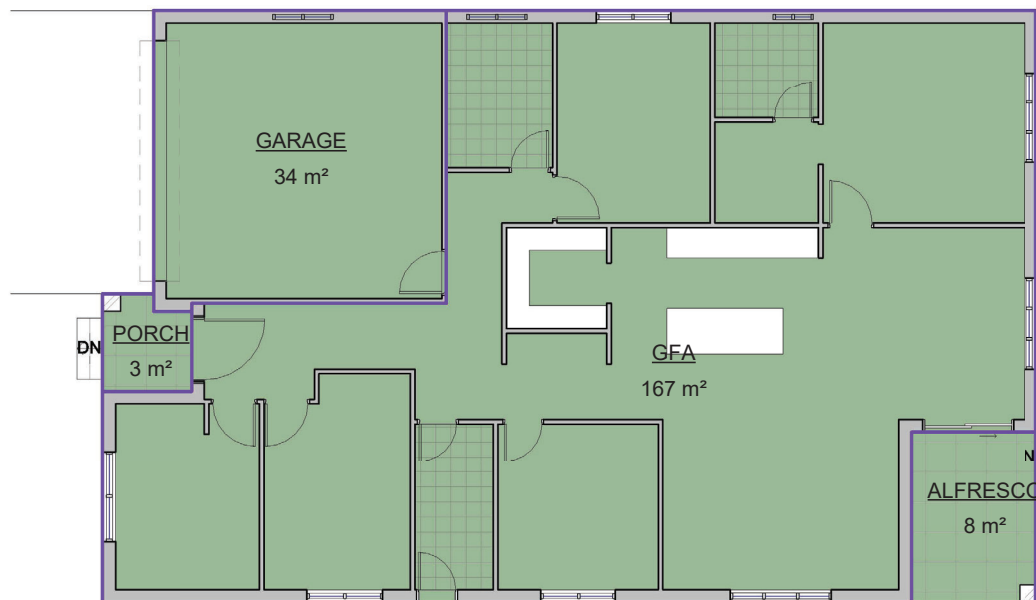

1 Ground Floor
1 : 100

Area Schedule (Gross Building)	
Name	Area

Ground Floor	
GFA	167 m²
GARAGE	34 m²
PORCH	3 m²
ALFRESCO	8 m²
Ground Floor: 4	213 m²
Grand total: 4	213 m²


REV	DATE	DESCRIPTION	BY
1	11-06-2026	CC ISSUE	



THIS DRAWING IS THE EXCLUSIVE PROPERTY OF THE DEVELOPER & THE REPRODUCTION OF ANY PART WITHOUT THE PRIOR WRITTEN CONSENT OF THE DEVELOPER IS A VIOLATION OF APPLICABLE LAWS. IN NO EVENT SHALL THE DEVELOPER BE HELD LIABLE FOR SPECIAL, COLLATERAL, INCIDENTAL OR CONSEQUENTIAL LIABILITY IN CONNECTION WITH THE USE OF THIS DIGITAL DATA ONCE RELEASED FROM THE DEVELOPER'S OFFICE. THIS DRAWING IS TO BE READ & UNDERSTOOD IN CONJUNCTION WITH THE STRUCTURAL, MECHANICAL, ELECTRICAL & / OR ANY OTHER CONSULTANT'S DOCUMENTATION AS MAY BE APPLICABLE TO THE PROJECT PRIOR TO THE START OF ANY WORKS AND FOR ITS DURATION.


PROJECT:
4 TRAVELLERS WAY
LOT 25 IN DP 1289262
No.04 TRAVELLERS WAYS
TAHMOOR nsw

DRAWING TITLE:
FLOOR AREA PLAN

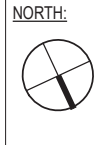

CC ISSUE			
LOT NO: 25	DATE: 1-07-2026	SCALE: 1 : 100	DRAWING No: CC.11
DRAWN BY: ROHIT	CHECKED BY: RH	ISSUED BY: Sudip Shreshta and Sanu Laxmi shreshta	
CLIENT NAME:			

OnBuild Certifiers Pty Ltd
Reference: 260036
Date: 27/07/2026
Andrew Soliman
Director/ Principal Certifier
BDC2940
Consultant who prepared this document
remains responsible for accuracy

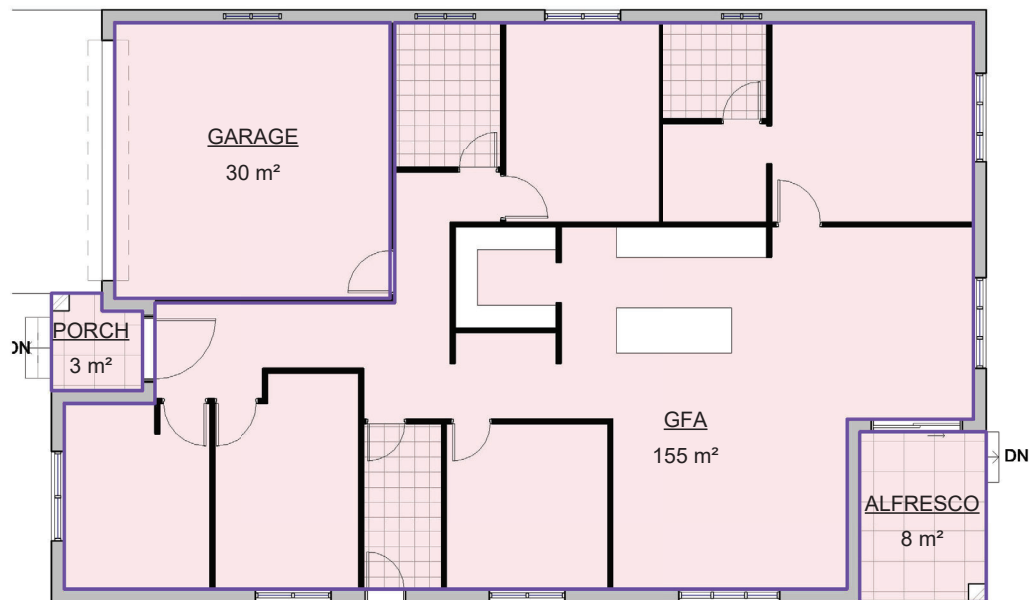

1 Ground Floor
1 : 100

Area Schedule (Rentable)	
Name	Area

Ground Floor	
GARAGE	30 m²
GFA	155 m²
ALFRESCO	8 m²
PORCH	3 m²
Ground Floor: 4	197 m²
Grand total: 4	197 m²


1	11-06-2026	CC ISSUE	
REV	DATE	DESCRIPTION	BY



THIS DRAWING IS THE EXCLUSIVE PROPERTY OF THE DEVELOPER & THE REPRODUCTION OF ANY PART WITHOUT THE PRIOR WRITTEN CONSENT OF THE DEVELOPER IS A VIOLATION OF APPLICABLE LAWS. IN NO EVENT SHALL THE DEVELOPER BE HELD LIABLE FOR SPECIAL, COLLATERAL, INCIDENTAL OR CONSEQUENTIAL LIABILITY IN CONNECTION WITH THE USE OF THIS DIGITAL DATA ONCE RELEASED FROM THE DEVELOPER'S OFFICE. THIS DRAWING IS TO BE READ & UNDERSTOOD IN CONJUNCTION WITH THE STRUCTURAL, MECHANICAL, ELECTRICAL & / OR ANY OTHER CONSULTANT'S DOCUMENTATION AS MAY BE APPLICABLE TO THE PROJECT PRIOR TO THE START OF ANY WORKS AND FOR ITS DURATION.

PROJECT:
4 TRAVELLERS WAY
LOT 25 IN DP 1289262
No.04 TRAVELLERS WAYS
TAHMOOR nsw


DRAWING TITLE:
RENTABLE AREA PLAN

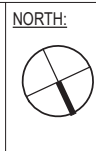

LOT NO: 25	DATE: 1-07-2026	SCALE: 1 : 100	DRAWING No: CC.12	REV: 1
DRAWN BY: ROHIT	CHECKED BY: RH			ISSUED BY:
CLIENT NAME: Sudip Shreshta and Sanu Laxmi shreshta				

CC ISSUE

OnBuild Certifiers Pty Ltd
Reference: 260036
Date: 27/07/2026
Andrew Soliman
Director/ Principal Certifier
BDC2940
Consultant who prepared this document
remains responsible for accuracy

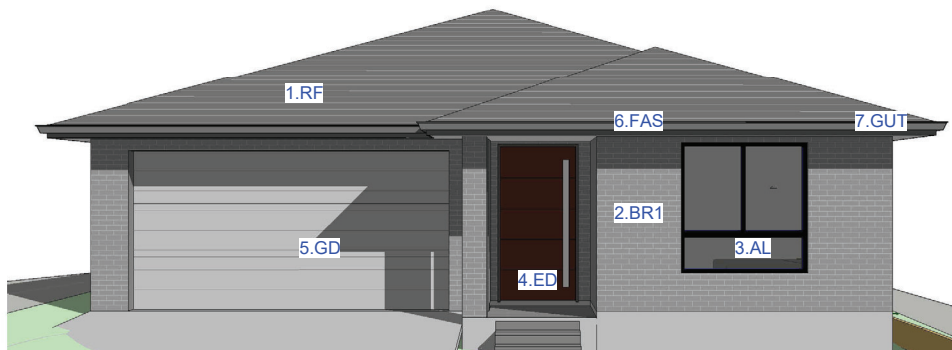

	1. RF	2. BR1	3. AL	4. ED	5. GD	6. FAS	7. GUT
	ROOF	MAIN WALLS	WINDOWS/ BALUSTRADE	MAIN DOOR	GARAGE DOOR	FASCIA	GUTTER
MATERIAL	Concrete TILE finish shale grey	SELECTED AUSTRAL OR PGH BRICK FROM BULDER RANGE	Manufacturer: ABM Door & Window Finish : Monument	TIMBER	COLORBOND Finish dover white or similar	Manufacturer: Colorbond® Finish : Monument	Manufacturer: Colorbond® Finish : Monument
COLOUR							

NOTE : ALL COLOURS SPECIFIED ARE INDICATIVE ONLY AND ARE SUBJECT TO VARIATION AND TO AVAILABILITY
ANY DISCREPANCY PLEASE FOLLOW AS PER RENDERED IMAGE

1	11-06-2026	CC ISSUE	
REV	DATE	DESCRIPTION	BY




THIS DRAWING IS THE EXCLUSIVE PROPERTY OF THE DEVELOPER & THE REPRODUCTION OF ANY PART WITHOUT THE PRIOR WRITTEN CONSENT OF THE DEVELOPER IS A VIOLATION OF APPLICABLE LAWS. IN NO EVENT SHALL THE DEVELOPER BE HELD LIABLE FOR SPECIAL, COLLATERAL, INCIDENTAL OR CONSEQUENTIAL LIABILITY IN CONNECTION WITH THE USE OF THIS DIGITAL DATA ONCE RELEASED FROM THE DEVELOPER'S OFFICE. THIS DRAWING IS TO BE READ & UNDERSTOOD IN CONJUNCTION WITH THE STRUCTURAL, MECHANICAL, ELECTRICAL & / OR ANY OTHER CONSULTANTS' DOCUMENTATION AS MAY BE APPLICABLE TO THE PROJECT PRIOR TO THE START OF ANY WORKS AND FOR ITS DURATION.

PROJECT:
4 TRAVELLERS WAY
LOT 25 IN DP 1289262
No.04 TRAVELLERS WAYS
TAHMOOR nsw


DRAWING TITLE:
COLOR SCHEDULE

NORTH:


LOT NO:	DATE:	SCALE:	DRAWING No:	REV:
25	1-07-2026			1
DRAWN BY:	CHECKED BY:	1 : 100	CC.13	ISSUED BY:
ROHIT	RH			
CLIENT NAME:				
Sudip Shreshta and Sanu Laxmi shreshta				

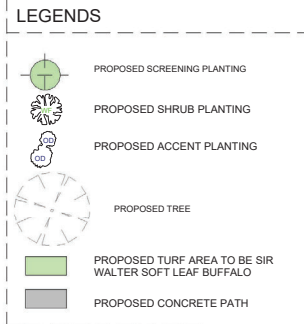

TREE TO BE REMOVED
WAY
Condition 21 of consent

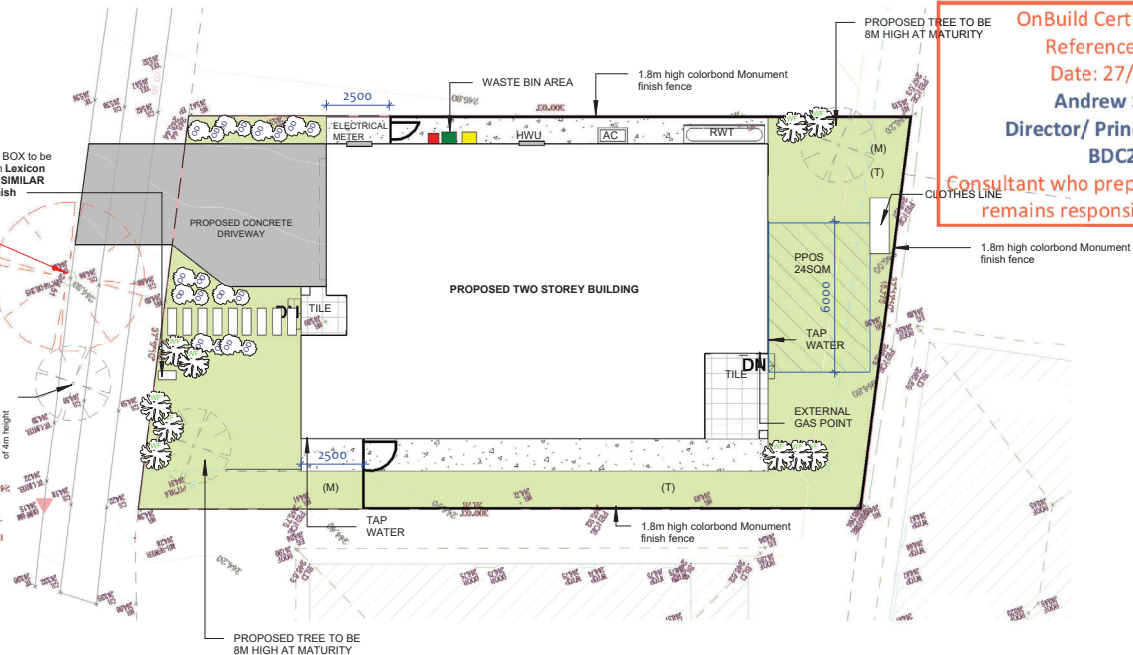

OnBuild Certifiers Pty Ltd
Reference: 260036
Date: 27/07/2026
Andrew Soliman
Director/ Principal Certifier
BDC2940
Consultant who prepared this document remains responsible for accuracy

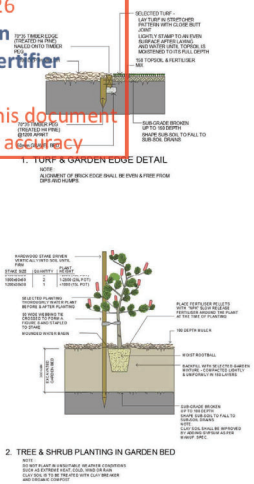

- GENERAL NOTES:**
- LANDSCAPE CONTRACTOR TO CHECK DA CONDITIONS AND STAMPED LANDSCAPE PLAN.
 - BEFORE COMMENCING WORKS TO ENSURE NO ADDITIONS/AMENDMENTS TO PLAN.
 - GARDEN BEDS IN OSD BASIN TO CONSIST OF NON FLOATABLE DECORATIVE GRAVEL.
 - REFER TO HYDRAULICS ENGINEERS PLAN FOR OSD DETAILS/FINAL LEVELS.
 - MULCHED PLANTING BEDS TO BE A MINIMUM DEPTH OF 75mm AS SELECTED.
 - CONTRACTOR'S RESPONSIBILITY TO CHECK AND ADJUST SOIL pH AS REQUIRED.
 - PROVIDE TIMBER EDGE AS A MINIMUM BENEATH FENCING/GATES TO DEFINE TURF AND GARDEN BEDS/PATHWAYS. EDGING TO BE PROVIDED TO ALL AREAS WHERE DIFFERING MATERIALS MEET i.e TURF/GARDEN, TURF/GRAVEL PATH ETC.
 - WEED MAT BENEATH GRAVEL PATHWAYS REQUIRED TO LIMIT MUD TRACKING.
 - PREMIUM ORGANIC GARDEN MIX TO BE USED.
 - ALL PLANTS TO BE HEALTHY AND VIGOROUS.
 - CONTRACTOR TO MAKE GOOD TURF ON NATURE STRIP POST CONSTRUCTION.
 - CONTRACTOR TO MAKE GOOD TURF ON NATURE STRIP POST CONSTRUCTION.
 - DO NOT SCALE ARCHITECTURAL SETOUT FROM LANDSCAPE DRAWING.
 - EXISTING TREE SPREAD APPROXIMATE ONLY. REFER TO TREE REPORT WHEN APPLICABLE.
 - SITE SURVEY PROVIDED BY OTHERS.
 - BUFFALO TURF PREFERRED OVER KIKUYU.

LANDSCAPE BASIX NOTE:
THE APPLICANT MUST PLANT INDIGENEOUS OR LOW WATER USE SPECIES OF VEGETATION THROUGHOUT 15 SQM OF THE SITE.

NOTE: BUILDER RESERVES THE RIGHT NOT TO UNDERTAKE NOR SUPPLY CERTIFICATE FOR OCCUPATION CERTIFICATE.
NOTE: TO AID COMPLIANCE WITH BASIX LEGISLATION, PLANTS (WHERE APPLICABLE) HAVE BEEN SELECTED FROM THE LOCAL CITY COUNCIL SHIRE PLANT LISTS.
NOTE: LOCATION OF SEWER MAINS/LINES, WATER PIPES, UNDERGROUND ELECTRICITY AND OTHER SERVICES MUST BE OBTAINED PRIOR TO COMMENCEMENT OF ANY WORK ON SITE.

CONTRACTORS NOTE: CALCULATED AREAS DETERMINED BY CAD AND HAVE BEEN ROUNDED UP FOR USE AS A GUIDE ONLY. ALLOW STANDARD PERCENTAGE FOR CUTTING AND WASTAGE. CONFIRM DIMENSIONS AND NUMBERS PRIOR TO QUOTING/ORDERING.

CC - LANDSCAPE PLAN

1 : 200

REAR LANDSCAPE area = 101.0m²
FRONT LANDSCAPE AREA = 61.0m²
TOTAL LANDSCAPE AREA = 162.0m²

PLANT SCHEDULE


Genus	Common Name	Qty	Pot size	Height	width
Trees					
Backhousia myrtifolia	Grey Myrtle	1	45L	6-10m	Dense feature tree with, green glossy foliage. Greenish yellow flowers in small terminal clusters.
Shrubs					
Bursaria Spinosa Var Sppinosa	Blackthorn, Boxthorn	8	140mm	1.5m	Thorny, wiry branches. Leaf size and shape varies with age. Small, white fragrant flowers.
Dodonea Visco ssp. Cuneata	Wedge-Leaft Hop Bush	6	140mm	1m	Compact growth. Sticky leaves taper to sharp point. Green fruit turns red and purple.
Indigofera Australis	Native Indigo	5	140mm	1m	Slender, erect. Pink to lilac pea flowers, numerous along stems.
Hedging & screening Plants					
Acmena smithii 'Cherry Surprise'	Lilly Pilly Cherry Surprise PBR	10	140mm	3m	It has attractive small dense green foliage that provides a continuous flush of cherry-red new growth nearly all year round. Small white starry flowers bloom in summer.



Bursaria spinosa var spinosa
Blackthorn, Boxthorn
Type: Shrub. Description: Thorny, wiry branches. Leaf size and shape varies with age. Small, white fragrant flowers. Height: 1m. All round Aug-Sept. Flowers: Spring. Propagation: from seed or layer cutting in Spring and Summer. Prune: after flowering, only to maintain shape.



Dodonea viscosa ssp. cuneata
Wedge-leaft Hop Bush
Type: Shrub. Description: Compact growth. Sticky leaves taper to sharp point. Green fruit turns red and purple. Height: 1m. All round Aug-Sept. Flowers: Spring. Propagation: from seed or layer cutting in Spring and Summer. Prune: trim lightly after flowering.

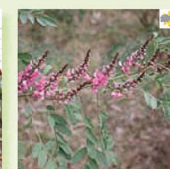

Indigofera australis
Native Indigo
Type: Shrub. Description: Slender, erect. Pink to lilac pea flowers, numerous along stems. Height: 1m. All round Aug-Sept. Flowers: Spring. Propagation: from seed or layer cutting in Spring and Summer. Prune: trim lightly after flowering.



Backhousia myrtifolia
Grey Myrtle
Type: Tree. Description: Dense feature tree with, green glossy foliage. Greenish yellow flowers in small terminal clusters. Height: 6-10m. Flowers: Nov-Dec. Propagation: saw seed in Spring. Prune: minimally.

Allocasuarina torulosa Forest She-oak
SIZE: Small Tree 4-7m x 4-6m. Moderate growth rate.
HABITAT: Widespread in a range of situations and soils.
FLOWERS: Inconspicuous, followed by woody cones.
FOLIAGE: Fine dark green needle-like, often reddish-ringed, which gives the plant one of its common names – Rose She-oak.
HARDINESS: Very hardy, once established, of frosts and droughts.
OTHER: Cones are eaten by Glossy Black Cockatoos. Attractive corky bark is another feature. Good bonsai.

CC ISSUE

REV	DATE	CC ISSUE	DESCRIPTION	BY
1	11-06-2026	CC ISSUE		

RUBY HOMES

THIS DRAWING IS THE EXCLUSIVE PROPERTY OF THE DEVELOPER & THE REPRODUCTION OF ANY PART WITHOUT THE PRIOR WRITTEN CONSENT OF THE DEVELOPER IS A VIOLATION OF APPLICABLE LAWS. IN NO EVENT SHALL THE DEVELOPER BE HELD LIABLE FOR SPECIAL, COLLATERAL, INCIDENTAL OR CONSEQUENTIAL LIABILITY IN CONNECTION WITH THE USE OF THIS DIGITAL DATA ONCE RELEASED FROM THE DEVELOPERS OFFICE. THIS DRAWING IS TO BE READ & UNDERSTOOD IN CONJUNCTION WITH THE STRUCTURAL, MECHANICAL, ELECTRICAL & OR ANY OTHER CONSULTANT'S DOCUMENTATION AS MAY BE APPLICABLE TO THE PROJECT PRIOR TO THE START OF ANY WORKS AND FOR ITS DURATION.


PROJECT:
4 TRAVELLERS WAY
Lot 25 in DP 1289262
No.04 TRAVELLERS WAYS
TAHMOOR NSW

DRAWING TITLE:
LANDSCAPE PLAN




LOT NO:	DATE:	SCALE:	DRAWING No:	REV:
25	1-07-2026	1 : 200	CC.14	1
DRAWN BY:	CHECKED BY:			ISSUED BY:
ROHIT	RH			
CLIENT NAME:				
Sudip Shreshta and Sanu Laxmi shreshta				

Consultant who prepared this document
remains responsible for accuracy

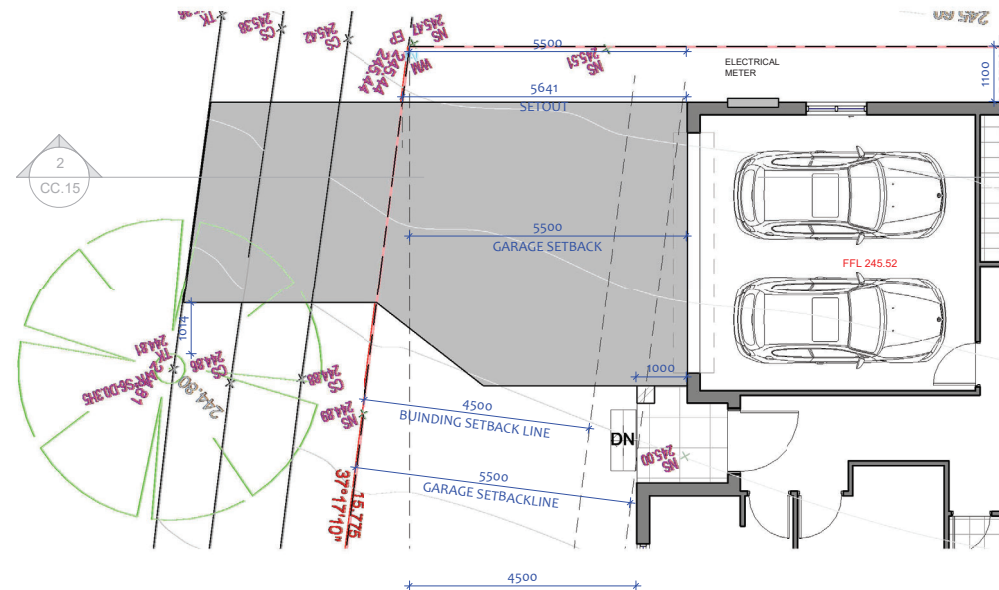

1 CC - DRIVEWAY PLAN
1 : 100

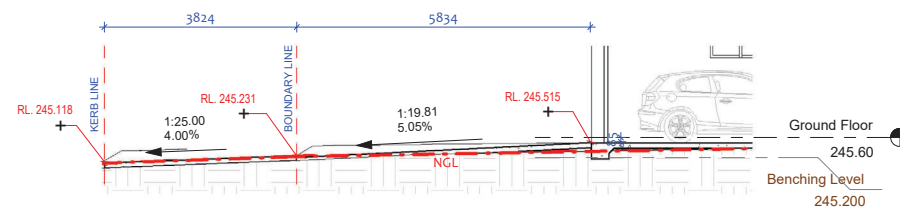

2 DRIVEWAY SECTION

[illegible]

THIS DRAWING IS THE EXCLUSIVE PROPERTY OF THE DEVELOPER & THE REPRODUCTION OF ANY PART WITHOUT THE PRIOR WRITTEN CONSENT OF THE DEVELOPER IS A VIOLATION OF APPLICABLE LAWS. IN NO EVENT SHALL THE DEVELOPER BE HELD LIABLE FOR SPECIAL, COLLATERAL, INCIDENTAL OR CONSEQUENTIAL LIABILITY IN CONNECTION WITH THE USE OF THIS DIGITAL DATA ONCE RELEASED FROM THE DEVELOPER'S OFFICE. THIS DRAWING IS TO BE READ & UNDERSTOOD IN CONJUNCTION WITH THE STRUCTURAL, MECHANICAL, ELECTRICAL & / OR ANY OTHER CONSULTANT DOCUMENTATION AS MAY BE APPLICABLE TO THE PROJECT PRIOR TO THE START OF ANY WORKS.

LOT 25 IN DP 1289262
No.04 TRAVELLERS WAYS
TAHMOOR nsw

DRIVEWAY DETAILS

25
DRAWN BY
ROH

CHECKED BY:
RH

1 : 100

CC 15

ISSUED BY:

Sudip Shreshta and Sanu Laxmi shreshta

CC ISSUE

ABCB HOUSING PROVISIONS : PART 10.2 WET AREA WATERPROOFING

10.2.1 Wet Areas

- Building elements in wet areas within a building must be protected with a waterproofing system.
- The waterproofing system in (1) must be either waterproof or water resistant in accordance with 10.2.2 to 10.2.6.

10.2.2 Shower Area (enclosed and unenclosed)

- For a shower area with a hob, step-down or level threshold, the following applies:
 - The floor of the **shower area** must be **waterproof**, including any hob or step-down (see Figure 10.2.2); and
 - The walls of the **shower area** must be **waterproof** not less than 1800 mm above the floor substrate (see Figure 10.2.2).
 - Wall junctions and joints within the **shower area** must be **waterproof** not less than 40 mm either side of the junction (see Figure 10.2.2).
 - Wall/floor junctions within the shower area must be **waterproof** (see Figure 10.2.2).
 - Penetrations within the shower area must be **waterproof**.
- A shower with a **preformed shower base** must also comply with the requirements of (1), except for (a) which is not applicable.

Figure 10.2.2: Extent of treatment for shower areas - concrete compressed fibre-cement and fibre-cement sheet floors.

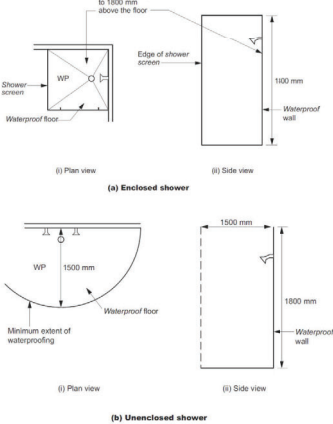


Figure Notes
 Wall/floor junction heights are to be as per 10.2.2 to 10.2.6 (as applicable).

Notes
 Where a shower is above a bath or spa, use requirements for shower.

10.2.3 Area outside shower area

- For concrete, compressed fibre-cement and fibre-cement sheet flooring, the floor of the room must be water resistant.
- For timber floors including particleboard, plywood and other timber based flooring materials, the floor of the room must be waterproof.
- Wall/floor junctions must be -
 - waterproof, and
 - where a flashing is used, the horizontal leg must be not less than 40 mm.

10.2.4 Areas adjacent to baths and spas without showers

- For areas adjacent to all baths and spas, the following applies:
 - For concrete, compressed fibre-cement and fibre-cement sheet flooring, the floor of the room must be water resistant.
 - For timber floors including particleboard, plywood and other timber based flooring materials, the floor of the room must be waterproof.
- Tap and spout penetrations must be waterproof where they occur in horizontal surfaces.
- For areas adjacent to non-freestanding baths and spas, the following applies:
 - Walls must be water resistant (see Figure 10.2.4a and Figure 10.2.4b):
 - to a height of not less than 150mm above the vessel, for the extent of the vessel, where the vessel is within 75mm of a wall and
 - for all exposed surfaces below vessel lip.
 - Wall junctions and joints must be water resistant within 150mm above a vessel for the extent of the vessel.
 - Wall/floor junctions must be waterproof for the extent of the vessel (see Figure 10.2.4a and Figure 10.2.4b).
- For inserted baths and spas, the following applies:
 - For floors and horizontal surfaces:
 - Any shelf area adjoining the bath or spa must be waterproof and include a waterstop under the vessel lip.
 - There are no requirements for the floor under a bath or spa.
 - For walls:
 - Waterproof to not less than 150mm above the lip of a bath or spa.
 - There are no requirements for the floor under a bath or spa.
 - For wall junctions and joints, the following applies:
 - Waterproof junctions within 150mm of a bath or spa.
 - There are no requirements for junctions and joints in walls beneath the lip of a bath or spa.
 - Tap and spout penetrations must be waterproof where they occur in horizontal surfaces.

Figure 10.2.4a: Areas adjacent to baths and spas without showers for concrete, compressed fibre-cement and fibre-cement sheet flooring




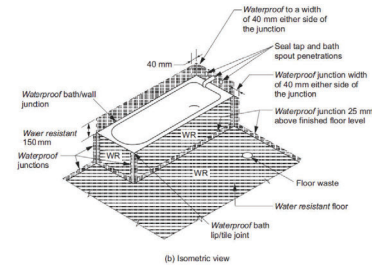



Figure 10.2.4b: Areas adjacent to baths and spas without showers for timber floors including particle-board, plywood and other floor materials

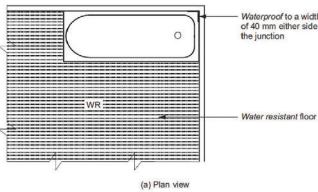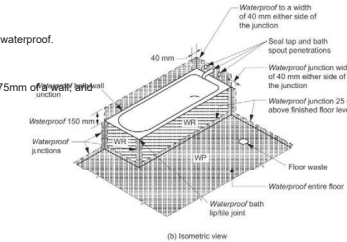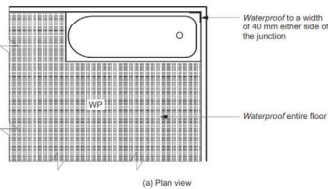

10.2.5 Other areas

- For walls adjoining other types of vessels (not sink, bath or tub) (b), the following applies:
 - Walls must be water resistant to a height of not less than 150mm above the vessel, for the extent of the vessel, where the vessel is within 75 mm of a wall (see Figure 10.2.5.)
 - Waterproof wall/floor junctions must be water resistant.
 - Waterproof tap and spout penetrations where they occur in surfaces required to be waterproof or water resistant.
- For laundries and WCs, the following applies:
 - The floor of the room must be water resistant.
 - Wall/floor junctions must be water resistant and where a flashing is used, the horizontal leg must be not less than 40 mm.
- For WCs with a handheld bidet spray installation, the following applies:
 - The floor of the room must be waterproof.
 - Walls must be -
 - waterproof in WC area within a 900 mm radius from the wall connection of the handheld bidet spray device to a height of not less than 150mm above the floor substrate; and
 - water resistant in WC area within a 900 mm radius from the wall connection of the handheld bidet device to not less than 1200 mm above the finished floor level of the WC.
 - Wall junctions within the WC area within 900 mm radius from the wall connection of the handheld bidet spray device must be waterproof.
 - Wall/floor junctions within the WC area within 1000 mm radius from the wall connection of the handheld bidet spray device must be waterproof.
 - Penetrations in the WC area must be waterproof.

Figure 10.2.5: Bath and vessel abutting wall - areas to be protected

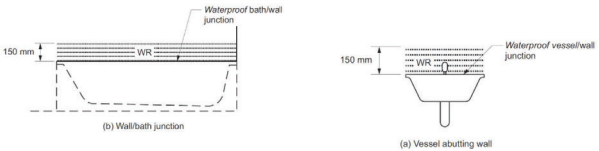

10.2.6 Waterproofing systems

- For the purposes of this Part, a waterproofing system is deemed -
 - waterproof, if it complies with (2); or
 - water resistant, if it complies with (3).
- For a waterproofing system required to be waterproof in accordance with 10.2.2 to 10.2.5, the materials nominated in 10.2.8 must be used.
- For a waterproofing system required to be water resistant in accordance with 10.2.2 to 10.2.5, the materials nominated in 10.2.9 must be used in conjunction with the materials in 10.2.10.

10.2.12 Construction of wet area floors - falls

Where a floor waste is installed -

- the minimum continuous fall of a floor plane to the waste must be 1:80; and
- the maximum continuous fall of a floor plane to the waste must be 1:50.

1	11-06-2026	CC ISSUE		
REV	DATE	DESCRIPTION	BY	

THIS DRAWING IS THE EXCLUSIVE PROPERTY OF THE DEVELOPER & THE REPRODUCTION OF ANY PART WITHOUT THE PRIOR WRITTEN CONSENT OF THE DEVELOPER IS A VIOLATION OF APPLICABLE LAWS. IN NO EVENT SHALL THE DEVELOPER BE HELD LIABLE FOR SPECIAL, COLLATERAL, INCIDENTAL OR CONSEQUENTIAL LIABILITY IN CONNECTION WITH THE USE OF THIS DIGITAL DATA ONCE RELEASED FROM THE DEVELOPERS OFFICE. THIS DRAWING IS TO BE READ & UNDERSTOOD IN CONJUNCTION WITH THE STRUCTURAL, MECHANICAL, ELECTRICAL & / OR ANY OTHER CONSULTANT'S DOCUMENTATION AS MAY BE APPLICABLE TO THE PROJECT PRIOR TO THE START OF ANY WORKS AND FOR ITS DURATION.

PROJECT:
4 TRAVELLERS WAY
 LOT 25 IN DP 1289262
 NO.04 TRAVELLERS WAYS
 TAHMOOR NSW

DRAWING TITLE:
WATERPROOFING DETAILS

NORTH:

LOT NO: 25	DATE: 1-07-2026	SCALE: 1 : 50	DRAWING No: CC.16	REV: 1
DRAWN BY: ROHIT	CHECKED BY: RH		ISSUED BY:	
CLIENT NAME: Sudip Shreshta and Sanu Laxmi shreshta				