


FOR CONSTRUCTION

LOT 38 IN DP 1312259
LOCATED AT 13 KLESENDORLFFE STREET, TAHMOOR NSW 2573.

Proposed Development Application for the Construction of a New Single-Storey Residential Dwelling with Double Garage and Associated Site Works on a Vacant Allotment

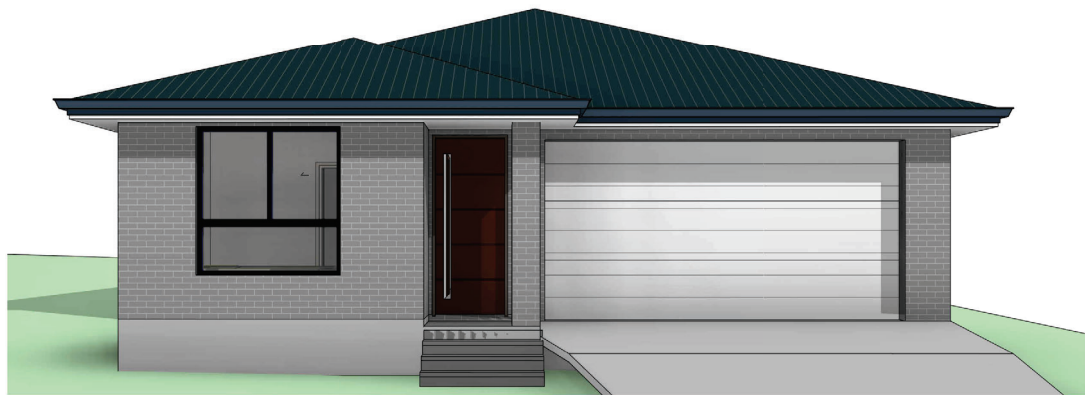

OnBuild Certifiers Pty Ltd
Reference: 260037
Date: 27/07/2026
GENERAL LEGEND
Andrew Soliman
Director/ Principal Certifier
BD 62940
Consultant who prepared this document remains responsible for accuracy

AC	AIR CONDITIONING UNIT
AL	ALUMINUM DOOR/ WINDOW
BS	BALUSTRADE TYPE
BR1, BR2, etc	BRICK FACE TYPE
CAP	METAL CAPPING
CD1, CD2, etc.	WALL CLADDING
CONC.	CONCRETE FLOOR
CPT	CARPET
CRT	CONCRETE ROOF TILES
CR1, CR2, etc.	CEMENT RENDER TYPE/ COLOUR
DP/S	DOWN PIPE
DW	DISH WASHER
ED	ENTRY DOOR
F	FRIDGE
FAS	FASCIA
FET	FEATURE TILE
FT, FT1, FT2, etc.	FLOOR TILES
FW	FLOOR WASTE
GD	GARAGE DOOR
GUT	GUTTER
HWU	HOT WATER UNIT
HYB	HYBRID FLOOR
L	LINEN
MR	METAL ROOF
MW	MICROWAVE OVEN
NGL	NATURAL GROUND LEVEL
OBS	OBSCURED GLASS
P	PANTRY
R	ROBE
RL	REDUCED LEVEL
RWH	RAIN WATER HEAD
RWT	RAIN WATER TANK
S	STORAGE
TOW	TOP OF WALL
TL	TIMBER LAMINATE
WC	WATER CLOSET
WM	WASHING MACHINE
SD	SMOKE DETECTOR

BASIC COMMITMENTS		Certificate number: 1836537S
		Date of issue: Monday, 09 March 2026
WATER		
LANDSCAPE	166m2	
TOILETS	4 STARS	
KITCHEN TAPS	4 STARS	
SHOWER HEADS	4 STAR (>4.5 but <=6 Umin)	
BASIN TAPS	4 STARS	
ALTERNATIVE WATER	5000L RAINWATER TANK	
ROOF WATER TO TANK	223m2	
ALT.WATER USES- TANK	LAUNDRY	
ALT. WATER USES - RETIC	ALL TOILETS + ONE OUTDOOR TAP	
SWIMMING POOL	N/A	
ENERGY		
HOT WATER	GAS INSTANTANEOUS - 5 STAR	
AIR-CON (HEATING)	3 PHASE DUCTED - EER 3.0-3.5	
AIR-CON (COOLING)	3 PHASE DUCTED - EER 3.0-3.5	
VENTILATION - BATHROOM	NONE/ NATURAL VENTILATION	
VENTILATION - KITCHEN	DUCTED - MANUAL SWITCH	
VENTILATION - LAUNDRY	INTERLOCKED WITH LIGHT	
PV SYSTEM	N/A	
COOKTOP	GAS	
OVEN	ELECTRIC	
CLOTHES DRYING	OUTDOOR CLOTHESLINE	
LIGHTING	DEDICATED LED	

CC ISSUE

LOT NO:	DATE:	SCALE:	DRAWING No:	REV:			
38	20-07-2026	As indicated	CC.01	1			
DRAWN BY:	CHECKED BY:	ISSUED BY:					
ROHIT	RH						
CLIENT NAME:							
Nirja Aryal Silwal & Ram Prasad Silwal							

NOTE: ALL IMAGES ARE FOR ILLUSTRATION ONLY AND ARE SUBJECT TO VARIATION AND TO AVAILABILITY OF MATERIALS.

REV	DATE	DESCRIPTION	BY
1	7-07-2026	Roof Changed to Colorbond - Ekta	

RUBY
HOMES

THIS DRAWING IS THE EXCLUSIVE PROPERTY OF THE DEVELOPER & THE REPRODUCTION OF ANY PART WITHOUT THE PRIOR WRITTEN CONSENT OF THE DEVELOPER IS A VIOLATION OF APPLICABLE LAWS. IN NO EVENT SHALL THE DEVELOPER BE HELD LIABLE FOR SPECIAL, COLLATERAL, INCIDENTAL OR CONSEQUENTIAL LIABILITY IN CONNECTION WITH THE USE OF THIS DIGITAL DATA ONCE RELEASED FROM THE DEVELOPER'S OFFICE. THIS DRAWING IS TO BE READ & UNDERSTOOD IN CONJUNCTION WITH THE STRUCTURAL, MECHANICAL, ELECTRICAL &/ OR ANY OTHER CONSULTANT'S DOCUMENTATION AS MAY BE APPLICABLE TO THE PROJECT PRIOR TO THE START OF ANY WORKS AND FOR ITS DURATION.

PROJECT:
LOT 38

13 KLESENDORLFFE STREET
TAHMOOR

DRAWING TITLE:
COVER SHEET

NORTH:

TERMITE SHEET

- TERMITE SHEET EXTENDS THROUGH THE ENTIRE MASONRY LEAF AND IS VISIBLE AT THE FINISHED FACE OF THE WALL.


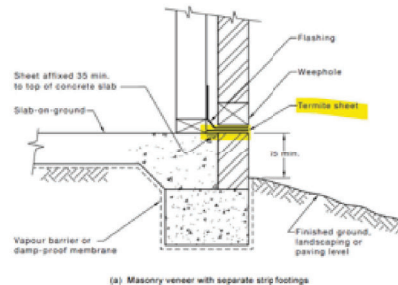


FIGURE 5.5 (in part) TYPICAL SHEET INSTALLATION TO EXTERNAL WALL WITH CONCRETE FLOORSLAB

DPC FOR BRICKS

DAMP-PROOF COURSE (DPC) TO EXTENDS THROUGH THE ENTIRE MASONRY LEAF AND NEED TO BE VISIBLE AT THE FINISHED FACE OF THE WALL FROM OUTSIDE

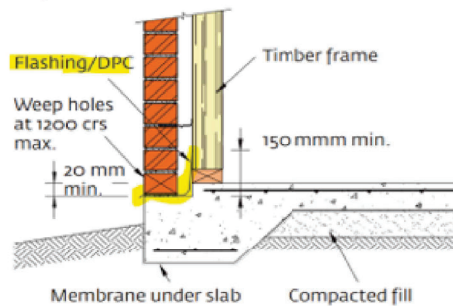

DEMOLITION

- AS 2601-2001 – DEMOLITION WORK

PLANTER BOX

REFER BELOW DETAILS FOR PLANTER BOX.



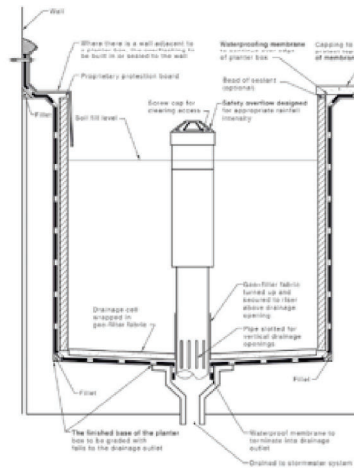


FIGURE 2.17 TYPICAL PLANTER BOX CONSTRUCTION

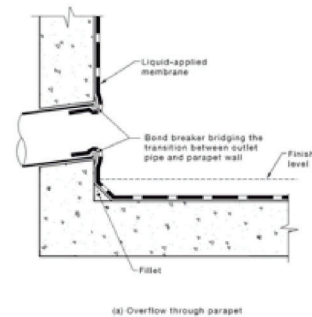

OVERFLOW TO BALCONY:

- SURFACE DRAIN & OVERFLOW TO BALCONY

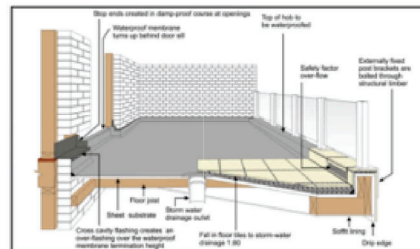

SWIMMING POOL

- PART 12.1.1 (H7D2) OF THE NCC VOLUME 2, AMENDMENT 1 - BUILDING CODE OF AUSTRALIA 2022 & HOUSING PROVISIONS STANDARD 2022
- AS 1926 PART 1-2012 – SWIMMING POOLS SAFETY- SAFETY BARRIERS FOR SWIMMING POOLS
- AS 1926 PART 2-2007 - SWIMMING POOL SAFETY- LOCATION OF SAFETY BARRIERS FOR SWIMMING POOLS (INCORPORATING AMENDMENTS 1 AND 2)
- AS 1926 PART 3-2010 – SWIMMING POOL SAFETY- WATER RECIRCULATION SYSTEMS (INCORPORATING AMENDMENT 1)

OnBuild Certifiers Pty Ltd

Reference: 260037

Date: 27/07/2026

Andrew Soliman

Director/ Principal Certifier

BDC2940

Consultant who prepared this document remains responsible for accuracy

REV	DATE	DESCRIPTION	BY
1	7-07-2026	Roof Changed to Colorbond - Ekta	



RUBY HOMES

THIS DRAWING IS THE EXCLUSIVE PROPERTY OF THE DEVELOPER & THE REPRODUCTION OF ANY PART WITHOUT THE PRIOR WRITTEN CONSENT OF THE DEVELOPER IS A VIOLATION OF APPLICABLE LAWS. IN NO EVENT SHALL THE DEVELOPER BE HELD LIABLE FOR SPECIAL, COLLATERAL, INCIDENTAL OR CONSEQUENTIAL LIABILITY IN CONNECTION WITH THE USE OF THIS DIGITAL DATA ONCE RELEASED FROM THE DEVELOPERS OFFICE. THIS DRAWING IS TO BE READ & UNDERSTOOD IN CONJUNCTION WITH THE STRUCTURAL, MECHANICAL, ELECTRICAL & / OR ANY OTHER CONSULTANT'S DOCUMENTATION AS MAY BE APPLICABLE TO THE PROJECT PRIOR TO THE START OF ANY WORKS AND FOR ITS DURATION.

PROJECT:
LOT 38

13 KLENSENDORLFFE STREET
TAHMOOR

DRAWING TITLE:
GENERAL NOTES

NORTH:

LOT NO:	DATE:	SCALE:	DRAWING No:	REV:
38	20-07-2026	1 : 2	CC.02B	1
DRAWN BY:	CHECKED BY:			ISSUED BY:
ROHIT	RH			

CLIENT NAME:
Nirja Aryal Silwal & Ram Prasad Silwal

KLENSENDORLFFE STREET

DA - SITE PLAN


1 : 200

1

2

DRIVEWAY SECTION

1 : 100

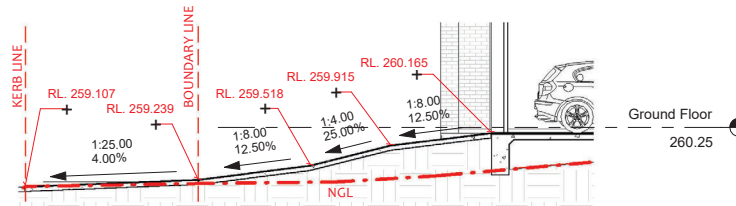

CODE COMPLIANCE TABLE				
Wollondilly Development Control Plan 2016 Volume 4 – Residential Development				
DESCRIPTION		COMPLIANCE		COMMENT
ELEMENT	CODE CONTROL	STANDARD	PROPOSED	
LAND ZONE	R2 – Low Density Residential			
LOT NO	LOT 38			
LOT AREA	451.2 m ²			
LOT WIDTH	Standard Lot Min. 6m at Building Line facing primary road	6.0m	14.85 m	YES
HEIGHT	MAX. Height	8.5m	5m (MAX.)	YES
FRONT SETBACK	FRONT SET BACK (Min. Setback from Primary Road)	4.5 m	4.5m	YES
REAR SET BACK (MIN.)	GROUND FLOOR	3m	7.5m	YES
	FIRST FLOOR	8m	NA	
SIDE SET BACK (MIN.)	GROUND FLOOR	0.9/0.9m	0.9/3.07m	YES
	FIRST FLOOR	0.9/0.9m	NA	
COVERAGE AREA	The total portion of the site covered by buildings shall not exceed 60% of the site area.	270SQM(60%)	180SQM(40%)	YES
PRIVATE OPEN SPACE		16m ²	324 m ²	YES
LANDSCAPE AREA			175.0 m ²	



APPROVED PLAN

Development Consent:
DA/2026/415/1

Determined: 20/5/2026

REV	DATE	DESCRIPTION	BY
1	10-03-2026	DA ISSUE	



THIS DRAWING IS THE EXCLUSIVE PROPERTY OF THE DEVELOPER & THE REPRODUCTION OF ANY PART WITHOUT THE PRIOR WRITTEN CONSENT OF THE DEVELOPER IS A VIOLATION OF APPLICABLE LAWS. IN NO EVENT SHALL THE DEVELOPER BE HELD LIABLE FOR SPECIAL, COLLATERAL, INCIDENTAL OR CONSEQUENTIAL LIABILITY IN CONNECTION WITH THE USE OF THIS DIGITAL DATA ONCE RELEASED FROM THE DEVELOPER'S OFFICE. THIS DRAWING IS TO BE READ & UNDERSTOOD IN CONJUNCTION WITH THE STRUCTURAL, MECHANICAL, ELECTRICAL &/OR ANY OTHER CONSULTANT'S DOCUMENTATION AS MAY BE APPLICABLE TO THE PROJECT PRIOR TO THE START OF ANY WORKS AND FOR ITS DURATION.

PROJECT:
LOT 38


13 KLENSENDORLFFE STREET
TAHMOOR

DRAWING TITLE:
**LOCATION PLAN
AND SITE PLAN**



LOT NO:	DATE:	SCALE:	<u>DRAWING</u> No:	REV:
38	10-03-2026	As indicated	DA.03A	1
DRAWN BY:	CHECKED BY:			ISSUED BY:
ROHIT	ROHIT			
CLIENT NAME:				
Nirja Aryal Silwal & Ram Prasad Silwal				

OnBuild Certifiers Pty Ltd
Reference: 260037
Date: 27/07/2026
Andrew Soliman
Director/ Principal Certifier
BDC2940
Consultant who prepared this document
remains responsible for accuracy

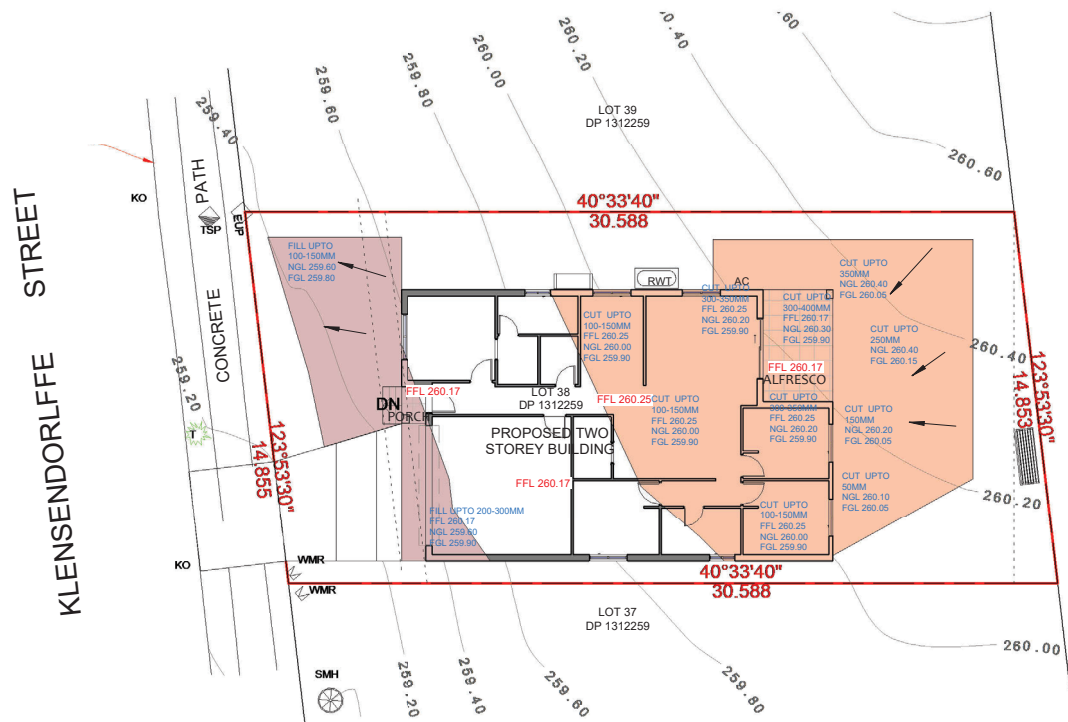

APPROVED PLAN
Development Consent:
DA/2026/415/1
Determined: 20/5/2026

Wollondilly
Shire Council

DA - CUT AND FILL PLAN
1 : 200

REV	DATE	DESCRIPTION	BY
1	10-03-2026	DA ISSUE	

RUBY HOMES

THIS DRAWING IS THE EXCLUSIVE PROPERTY OF THE DEVELOPER & THE REPRODUCTION OF ANY PART WITHOUT THE PRIOR WRITTEN CONSENT OF THE DEVELOPER IS A VIOLATION OF APPLICABLE LAWS. IN NO EVENT SHALL THE DEVELOPER BE HELD LIABLE FOR SPECIAL, COLLATERAL, INCIDENTAL OR CONSEQUENTIAL LIABILITY IN CONNECTION WITH THE USE OF THIS DIGITAL DATA ONLY. RELEASED FROM THE DEVELOPER'S OFFICE. THIS DRAWING IS TO BE READ & UNDERSTOOD IN CONJUNCTION WITH THE STRUCTURAL, MECHANICAL, ELECTRICAL &/OR ANY OTHER CONSULTANT'S DOCUMENTATION AS MAY BE APPLICABLE TO THE PROJECT PRIOR TO THE START OF ANY WORKS AND FOR ITS DURATION.

PROJECT:
LOT 38


13 KLENSENDORLFFE STREET
TAHMOOR

DRAWING TITLE:
SITE CUT/FILL PLAN



LOT NO:	DATE:	SCALE:	DRAWING No:	REV:
38	10-03-2026	1 : 200	DA.03B	1
DRAWN BY:	CHECKED BY:			ISSUED BY:
ROHIT	ROHIT			
CLIENT NAME: Nirja Aryal Silwal & Ram Prasad Silwal				

KLENSENDORLFFE STREET

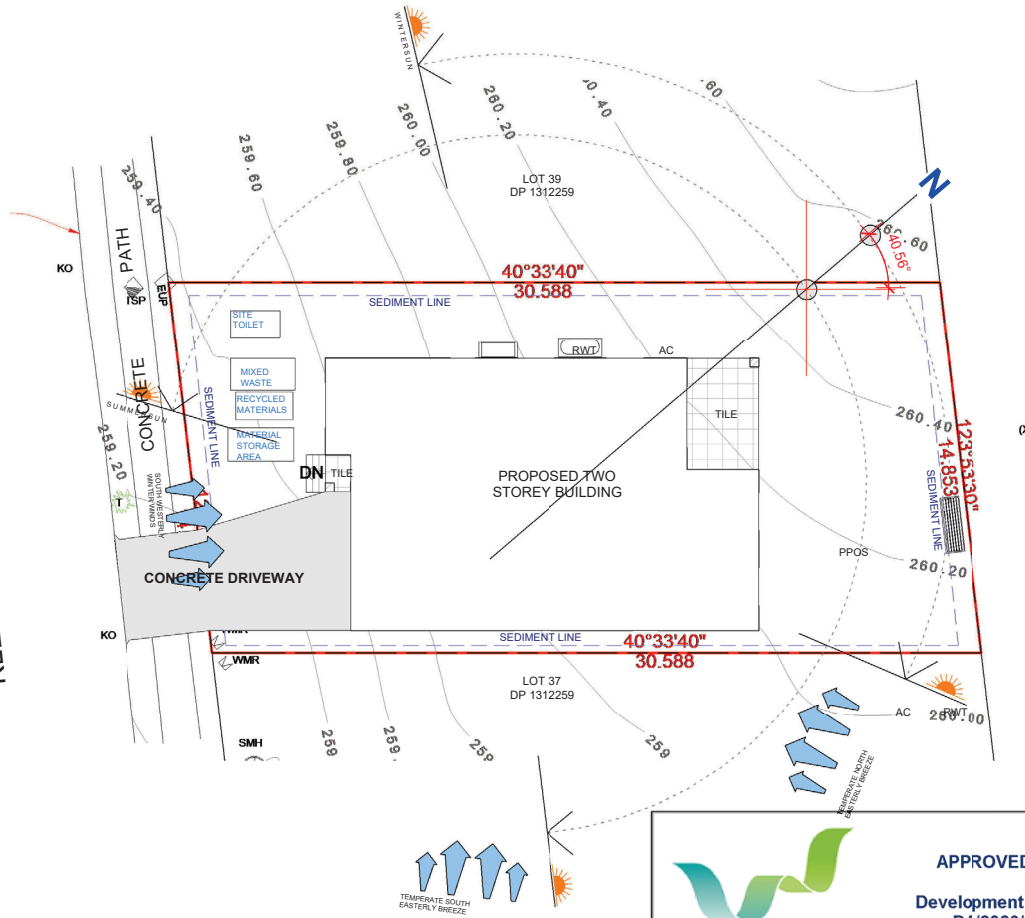

APPROVED PLAN





Development Consent:
DA/2026/415/1

Determined: 20/5/2026

Wollondilly Shire Council

DA - SITE ANALYSIS AND SEDIMENT CONTROL PLAN

1 : 200

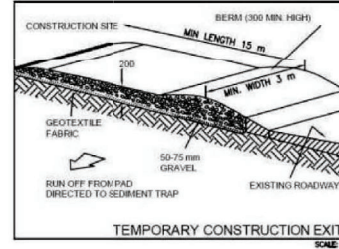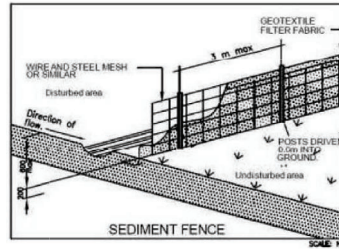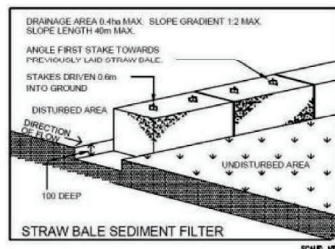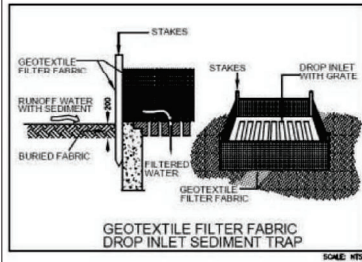

SD-6-9 GEOTEXTILE INLET FILTER

- 1) FABRICATE A SEDIMENT BARRIER MADE FROM GEOTEXTILE. REFER SD-6-7 FOR DETAILS.
- 2) SUPPORT GEOTEXTILE WITH MESH TIED TO POSTS AT 1 m CTR.
- 3) DO NOT COVER INLET WITH GEOTEXTILE.

REV	DATE	DESCRIPTION	BY
1	10-03-2026	DA ISSUE	

RUBY HOMES

THIS DRAWING IS THE EXCLUSIVE PROPERTY OF THE DEVELOPER & THE REPRODUCTION OF ANY PART WITHOUT THE PRIOR WRITTEN CONSENT OF THE DEVELOPER IS A VIOLATION OF APPLICABLE LAWS. IN NO EVENT SHALL THE DEVELOPER BE HELD LIABLE FOR SPECIAL, COLLATERAL, INCIDENTAL OR CONSEQUENTIAL LIABILITY IN CONNECTION WITH THE USE OF THIS DIGITAL DATA ONCE RELEASED FROM THE DEVELOPER'S OFFICE. THIS DRAWING IS TO BE READ & UNDERSTOOD IN CONJUNCTION WITH THE STRUCTURAL, MECHANICAL, ELECTRICAL & / OR ANY OTHER CONSULTANT'S DOCUMENTATION AS MAY BE APPLICABLE TO THE PROJECT PRIOR TO THE START OF ANY WORKS AND FOR ITS DURATION.

PROJECT:
LOT 38

13 KLENSENDORLFFE STREET
TAHMOOR

DRAWING TITLE:
SITE ANALYSIS AND SEDIMENT CONTROL



LOT NO:	DATE:	SCALE:	DRAWING No:	REV:
38	10-03-2026	As indicated	DA.04	1
DRAWN BY:	CHECKED BY:	CLIENT NAME:	ISSUED BY:	
ROHIT	ROHIT	Nirja Aryal Silwal & Ram Prasad Silwal		

- OnBuild Certifiers Pty Ltd**
- SEDIMENT AND EROSION NOTES:**
- THIS PLAN IS TO BE READ IN CONJUNCTION WITH SEDIMENT AND EROSION CONTROL DETAILS AS ATTACHED.
 - THE CONTRACTOR SHALL IMPLEMENT ALL SOIL EROSION AND SEDIMENT CONTROL MEASURES AS NECESSARY AND TO THE SATISFACTION OF COUNCIL PRIOR TO THE COMMENCEMENT OF WORK AND DURING CONSTRUCTION. NO DISTURBANCE TO THE SITE SHALL BE PERMITTED OTHER THAN IN THE IMMEDIATE AREA OF THE WORK AND NO MATERIAL SHALL BE REMOVED FROM THE SITE WITHOUT COUNCIL'S APPROVAL. ALL SEDIMENT AND EROSION CONTROL DEVICES TO BE INSTALLED AND MAINTAINED IN ACCORDANCE WITH STANDARDS OUTLINED IN NSW DEPARTMENT OF HOUSING "MANAGING URBAN STORMWATER SOLES AND CONSTRUCTIONS". TOPSOIL SHALL BE STRIPPED AND STOCKPILED OUTSIDE HAZARDOUS AREAS SUCH AS DRAINAGE LINES. THIS TOPSOIL IS TO BE RESPIRED LATER ON AREAS TO BE REVEGETATED AND STABILISED ONLY. (I.E ALL FOOTPATHS, BATTERS, SITE REGARDING AREAS, BASINS AND CATCH DRAINS). TOPSOIL SHALL NOT BE RESPIRED ON ANY OTHER AREAS UNLESS SPECIALLY INSTRUCTED BY THE SUPERINTENDENT. IF THEY ARE TO REMAIN FOR LONGER THAN ONE MONTH STOCKPILES SHALL BE PROTECTED FROM EROSION BY COVERING THEM WITH A MULCH AND HYDROSEEDING AND, IF NECESSARY, BY LOCATING BANKS OR DRAINS DOWNSTREAM OF A STOCKPILE TO RETARD SILT LADEN RUNOFF.
 - THE CONTRACTOR SHALL REGULARLY MAINTAIN ALL SEDIMENT AND EROSION CONTROL DEVICES AND REMOVE ACCUMULATED SILT FROM SUCH DEVICES SUCH THAT MORE THAN 60% OF THEIR CAPACITY LOST. ALL THE SILTS TO BE PLACED OUTSIDE THE LIMIT OF WORKS. THE PERIOD FOR MAINTAINING THESE DEVICES SHALL BE AT LEAST UNTIL ALL DISTURBED AREAS ARE REVEGETATED AND FURTHER AS MAY BE DIRECTED BY THE SUPERINTENDENT OR COUNCIL.
 - LAY TURF STRIP (MIN 300 mm WIDE) ON 100 mm TOPSOIL WITH 1.0 m LONG RETURNS EVERY 6.0m BEHIND ALL KERB AT THE TOP OF ALL BATTERS AND AROUND STRUCTURES IMMEDIATELY AFTER BACKFILLING OR FORMATION.
 - THE CONTRACTOR SHALL GRASS SEED ALL DISTURBED AREAS WITH AN APPROVED MIX AS SS0N AS PRACTICABLE AFTER COMPLETION OF EARTHWORKS AND REGRADING.
 - VEHICULAR TRAFFIC SHALL BE CONTROLLED DURING CONSTRUCTION CONFIRMING ACCESS WHERE POSSIBLE TO NOMINATED STABILISED ACCESS POINTS.
 - WHEN ANY DEVICES ARE TO BE HANDED OVER TO COUNCIL, THEY SHALL BE IN CLEAN AND STABLE CONDITION.
 - THE CONTRACTOR SHALL IMPLEMENT DUST CONTROL BY REGULAR WETTING DOWN (BUT NOT SATURATING) DISTURBED AREA.
 - PROVIDE AND MAINTAIN SILT TRAPS AROUND ALL SURFACE INLET PITS UNTL CATCHMENT IS REVEGETATED OR PAVED.
 - REVEGETATE ALL TRENCHES IMMEDIATELY UPON COMPLETION OF BACKFILLING.
 - ALL DRAINAGE PIPE INLETS TO BE CAPPED UNTIL:
 - A) DOWNPIPES CONNECTED
 - B) PITS CONSTRUCTED & PROTECTED WITH SILT BARRIER

SITE WORKS NOTES

1. ORIGIN OF LEVELS PROVIDED BY SURVEYOR
2. THE BUILDER SHALL VERIFY ALL DIMENSIONS AND EXISTING LEVELS ON SITE PRIOR TO THE COMMENCEMENT OF WORK AND ANY DISCREPANCIES SHALL BE REPORTED TO THE SURVEYOR / ENGINEER
3. TOPSOIL SHALL BE STRIPPED FROM THE CONSTRUCTION AREA AND STOCKPILED ON SITE, TO BE LATER SPREAD OR DISPOSED OFF SITE AS DIRECTED BY SUPERVISOR / ENGINEER
4. ALL TRENCH BACKFILL MATERIAL SHALL BE COMPACTED TO THE SAME DENSITY AS THE ADJACENT MATERIAL
5. ALL SERVICE TRENCHES UNDER VEHICULAR PAVEMENTS SHALL BE BACKFILLED WITH SAND OR APPROVED GRANULAR MATERIALS TO THE UNDERSIDE OF THE PAVEMENT, AND COMPACTED TO BRIDGING MAXIMUM DRY DENSITY, IN ACCORDANCE WITH AS 12891.1.

TEMPORARY 1.8M HIGH WIRE ML FENCE WITH DUSTPROOF MESH APPLIED TO FULL HEIGHT TO BOUNDARIES AS REQUIRED

LOCATION OF WASTE BINS

SEDIMENT FENCE AS REQUIRED

GRAVEL ACCESS

SILT ACCESS AREA TO BE USED FOR WASHDOWN AREA

FOOTPATH CLEAN AND CLEAR AT ALL TIMES

LOCATION OF STOCKPILE MATERIAL

MATERIAL STORAGE AREA


TEMPORARY TOILETS

INSTALL TEMPORARY SEDIMENT BARRIERS TO ALL INLET PITS LIKELY TO COLLECT SILT LADEN WATER, TO COUNCIL'S REQUIREMENTS.

DA ISSUE

OnBuild Construction Ltd
Referenced by:
Date: 20-07-2026
Andrew Solomon
Director/ Principal Engineer
BPC3540
Consultant who prepared this document remains responsible for accuracy

IMPORTANT NOTES:
 ALL DIMENSIONS AND NOTES ON ALL PLANS MUST BE CHECKED AND VERIFIED BY BUILDERS AND OWNER PRIOR TO COMMENCEMENT OF ANY BUILDING WORKS. TO CLARIFY AND CONFIRM WITH CONSTRUCTION COMPANY FOR DISCREPANCIES ON ALL DOCUMENTS AND PLANS PROVIDED FOR CONSTRUCTION. ANY WORK INDICATED ON THE PLAN BUT NOT IN CONTRACT, VARIATION TO PLANS. SPECIFICATIONS MAY NOT BE THE RESPONSIBILITY OF THE BUILDER. END USER TO VERIFY PLANS CURRENT BCA AND AUSTRALIAN STANDARDS. WINDOWS TO COMPLY WITH 3.9.3.5 OF THE BCA.

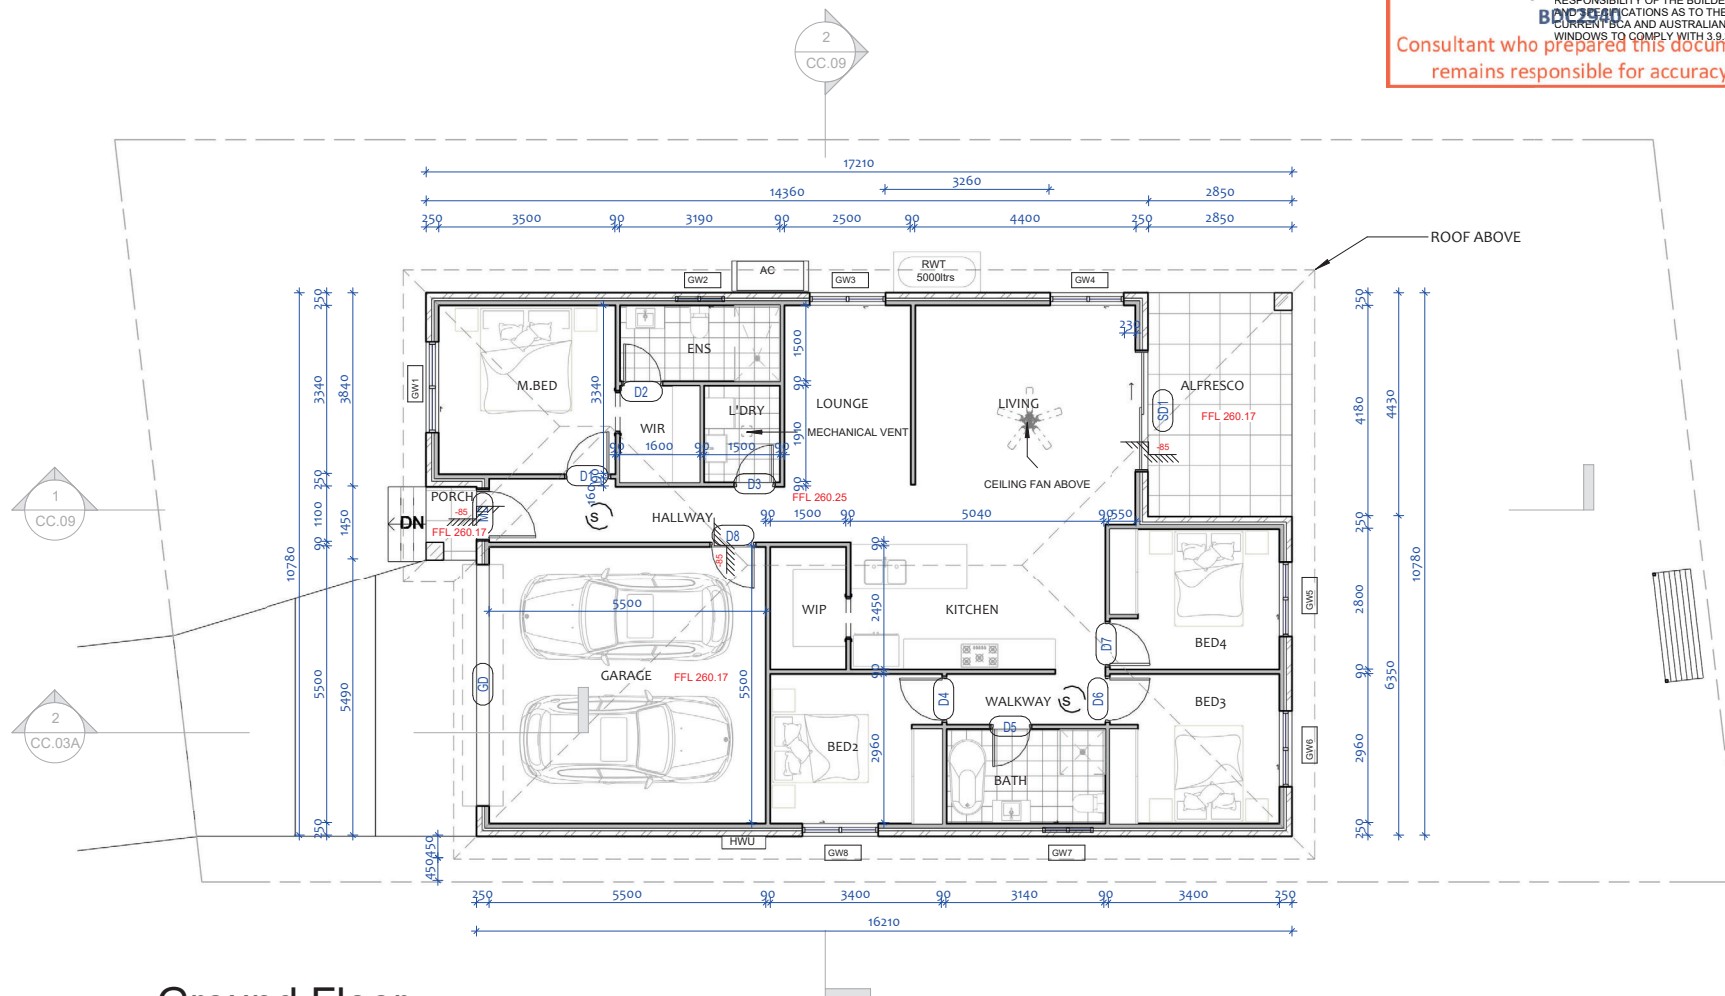

1 **Ground Floor**
 1 : 100

NOTE: PLEASE REFER TO TENDER FOR ALL INCLUSIONS.

REV	DATE	DESCRIPTION	BY
1	7-07-2026	Roof Changed to Colorbond - Ekta	

RUBY HOMES

THIS DRAWING IS THE EXCLUSIVE PROPERTY OF THE DEVELOPER & THE REPRODUCTION OF ANY PART WITHOUT THE PRIOR WRITTEN CONSENT OF THE DEVELOPER IS A VIOLATION OF APPLICABLE LAWS. IN NO EVENT SHALL THE DEVELOPER BE HELD LIABLE FOR SPECIAL COLLATERAL, INCIDENTAL OR CONSEQUENTIAL LIABILITY IN CONNECTION WITH THE USE OF THIS DIGITAL DATA ONCE RELEASED FROM THE DEVELOPER'S OFFICE. THIS DRAWING IS TO BE READ & UNDERSTOOD IN CONJUNCTION WITH THE STRUCTURAL, MECHANICAL, ELECTRICAL &/OR ANY OTHER CONSULTANT'S DOCUMENTATION AS MAY BE APPLICABLE TO THE PROJECT PRIOR TO THE START OF ANY WORKS AND FOR ITS DURATION.

PROJECT:
LOT 38
13 KLENSENDORLFFE STREET
TAHMOOR


DRAWING TITLE:
GROUND FLOOR PLAN



LOT NO:	DATE:	SCALE:	DRAWING No:	REV:
38	20-07-2026	1 : 100	CC.05	1
DRAWN BY:	CHECKED BY:			ISSUED BY:
ROHIT	RH			
CLIENT NAME: Nirja Aryal Silwal & Ram Prasad Silwal				

OnBuild Construction Ltd
Referenced by:
Date: 10-03-2026
Andrew Solomon
Director/ Principal Engineer
BAC 35401
Consultant who prepared this document remains responsible for accuracy

IMPORTANT NOTES:
ALL DIMENSIONS AND NOTES ON ALL PLANS MUST BE CHECKED AND VERIFIED BY BUILDERS AND OWNER PRIOR TO COMMENCEMENT OF ANY BUILDING WORKS. TO CLARIFY AND CONFIRM WITH CONSTRUCTION COMPANY FOR DISCREPANCIES ON ALL DOCUMENTS AND PLANS PROVIDED FOR CONSTRUCTION. ANY WORK INDICATED ON THE PLAN BUT NOT IN CONTRACT, VARIATION TO PLANS, SPECIFICATIONS MAY NOT BE THE RESPONSIBILITY OF THE BUILDER. END USER TO VERIFY PLANS CURRENT BCA AND AUSTRALIAN STANDARDS. WINDOWS TO COMPLY WITH 3.9.3.5 OF THE BCA.

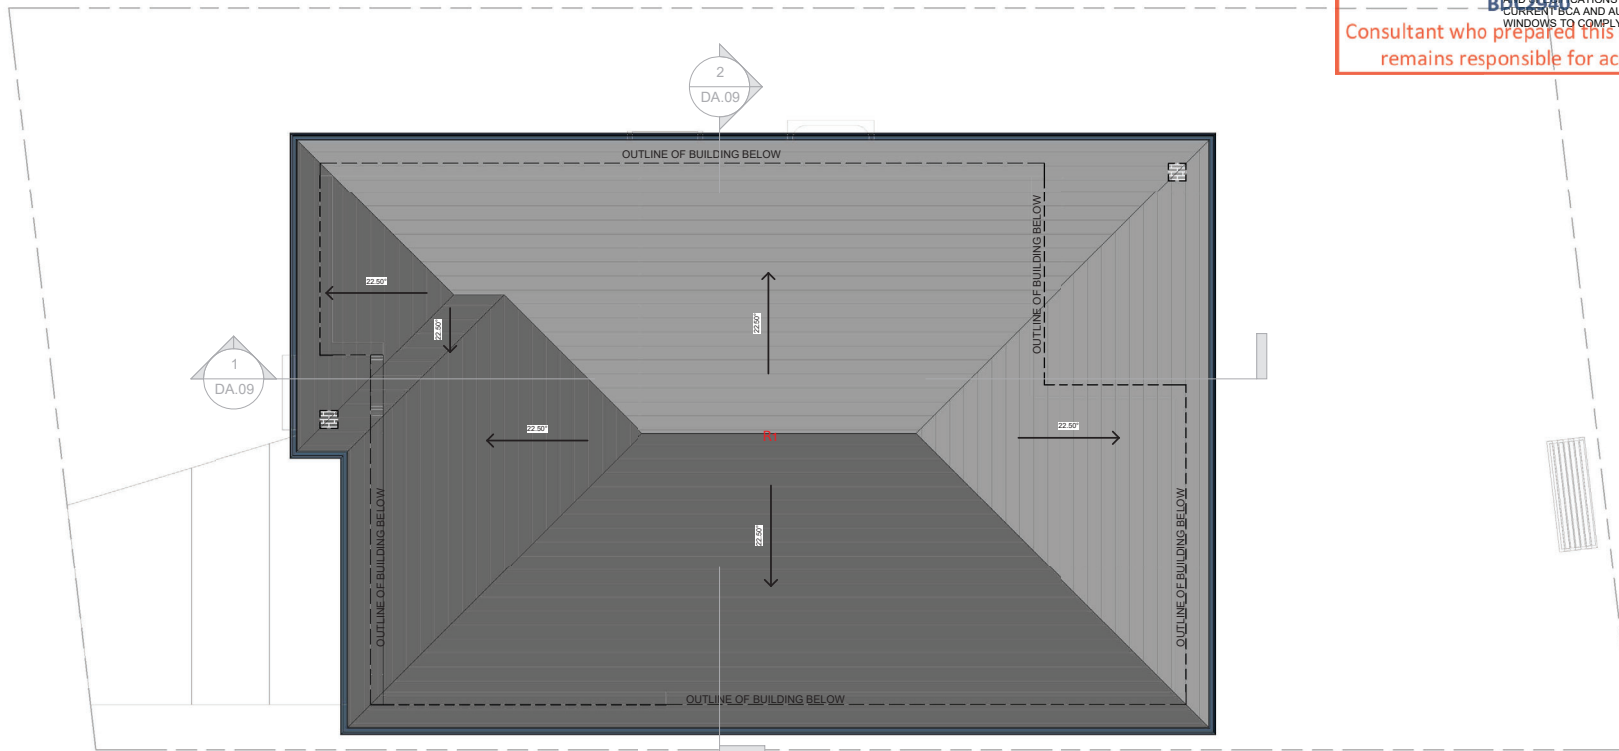

1 Level 1
1 : 100

Roof Schedule			
Mark	Base Level	Area	Comments
R1	Ground Ceiling	223 m ²	Concrete Tile Roof



APPROVED PLAN
Development Consent:
DA/2026/415/1
Determined: 20/5/2026

REV	DATE	DESCRIPTION	BY
1	10-03-2026	DA ISSUE	



THIS DRAWING IS THE EXCLUSIVE PROPERTY OF THE DEVELOPER & THE REPRODUCTION OF ANY PART WITHOUT THE PRIOR WRITTEN CONSENT OF THE DEVELOPER IS A VIOLATION OF APPLICABLE LAWS. IN NO EVENT SHALL THE DEVELOPER BE HELD LIABLE FOR SPECIAL, COLLATERAL, INCIDENTAL OR CONSEQUENTIAL LIABILITY IN CONNECTION WITH THE USE OF THIS DIGITAL DATA ONCE RELEASED FROM THE DEVELOPER'S OFFICE. THIS DRAWING IS TO BE READ & UNDERSTOOD IN CONJUNCTION WITH THE STRUCTURAL, MECHANICAL, ELECTRICAL & / OR ANY OTHER CONSULTANTS' DOCUMENTATION AS MAY BE APPLICABLE TO THE PROJECT PRIOR TO THE START OF ANY WORKS AND FOR ITS DURATION.

PROJECT:
LOT 38


13 KLENSENDORLFFE STREET
TAHMOOR

DRAWING TITLE:
ROOF PLAN




DA ISSUE					
LOT NO: 38	DATE: 10-03-2026	SCALE: 1 : 100	DRAWING No: DA.06	REV: 1	ISSUED BY:
DRAWN BY: ROHIT	CHECKED BY: ROHIT	CLIENT NAME: Nirja Aryal Silwal & Ram Prasad Silwal			

OnBuild Certifiers Pty Ltd
Reference: 260037
Date: 27/07/2026
Andrew Soliman
Director/ Principal Certifier
BDC2940
Consultant who prepared this document
remains responsible for accuracy

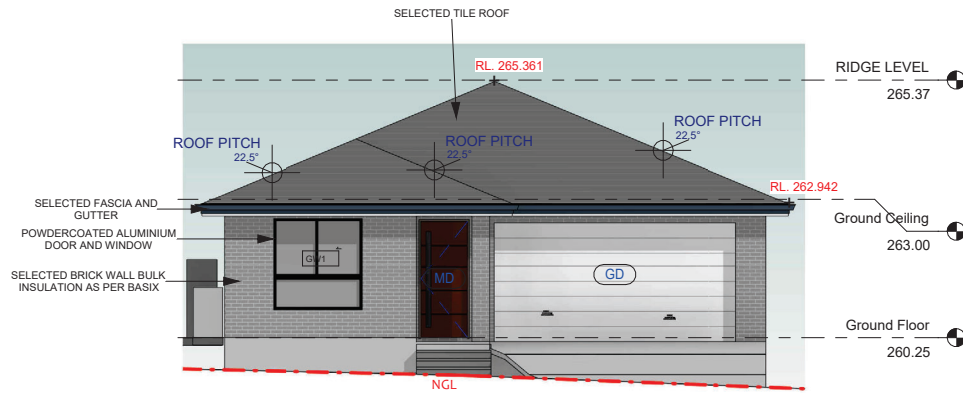

1 South-West Elevation
1 : 100

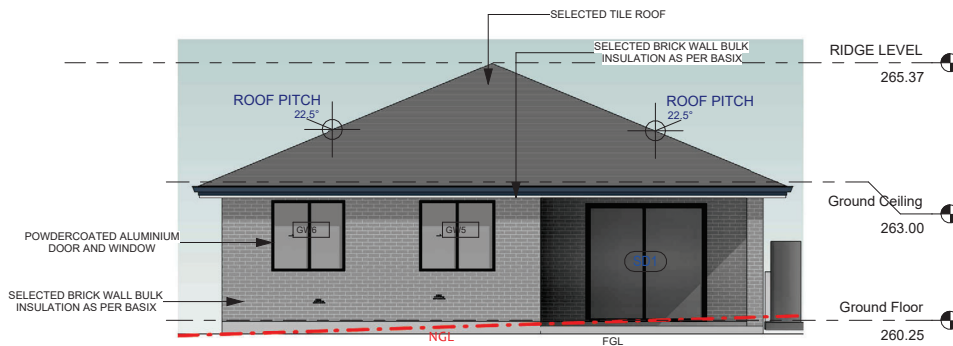

2 North-East Elevation
1 : 100

Window Schedule 1					
Mark	Height	Width	Sill Height	Head Height	Description

Ground Floor

GW1	1850	1800	550	2400	SLIDING
GW2	600	1000	1800	2400	SLIDING
GW3	1400	1500	1000	2400	SLIDING
GW4	1400	1500	1000	2400	SLIDING
GW5	1400	1500	1000	2400	SLIDING
GW6	1400	1500	1000	2400	SLIDING
GW7	600	1000	1800	2400	SLIDING
GW8	1400	1500	1000	2400	SLIDING

Ground Floor: 8

Door Schedule 1				
Mark	Height	Width	Count	Description


Ground Floor

D1	2340	820	1	FLUSH DOOR
D2	2340	720	1	FLUSH DOOR
D3	2340	720	1	FLUSH DOOR
D4	2340	820	1	FLUSH DOOR
D5	2340	720	1	FLUSH DOOR
D6	2340	820	1	FLUSH DOOR
D7	2340	820	1	FLUSH DOOR
D8	2340	820	1	FLUSH DOOR
GD	2400	4800	1	GARAGE DOOR
MD	2340	920	1	SOLID CORE DOOR
SD1	2300	2400	1	SLIDING DOOR

Ground Floor: 11



REV	DATE	DESCRIPTION	BY
1	10-03-2026	DA ISSUE	

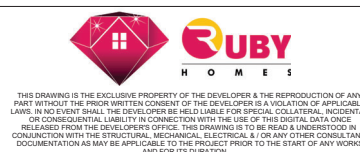


PROJECT:
LOT 38

13 KLENSENDORLFFE STREET
TAHMOOR


DRAWING TITLE:
ELEVATION 01

DA ISSUE					
NORTH:	LOT NO: 38	DATE: 10-03-2026	SCALE: 1 : 100	DRAWING No: DA.07	REV: 1
	DRAWN BY: ROHIT	CHECKED BY: ROHIT		ISSUED BY:	
	CLIENT NAME: Nirja Aryal Silwal & Ram Prasad Silwal				

OnBuild Certifiers Pty Ltd
Reference: 260037
Date: 27/07/2026
Andrew Soliman
Director/ Principal Certifier
BDC2940
Consultant who prepared this document
remains responsible for accuracy

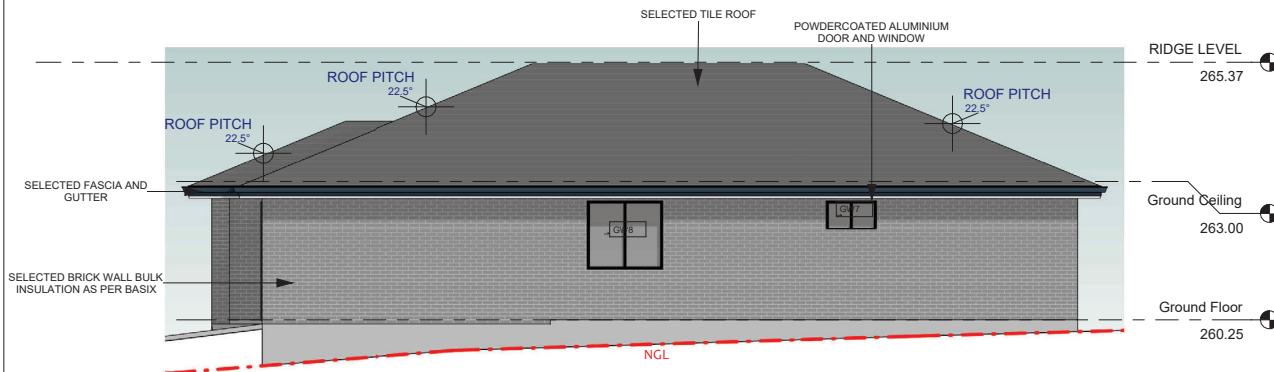

1 South-East Elevation
1 : 100

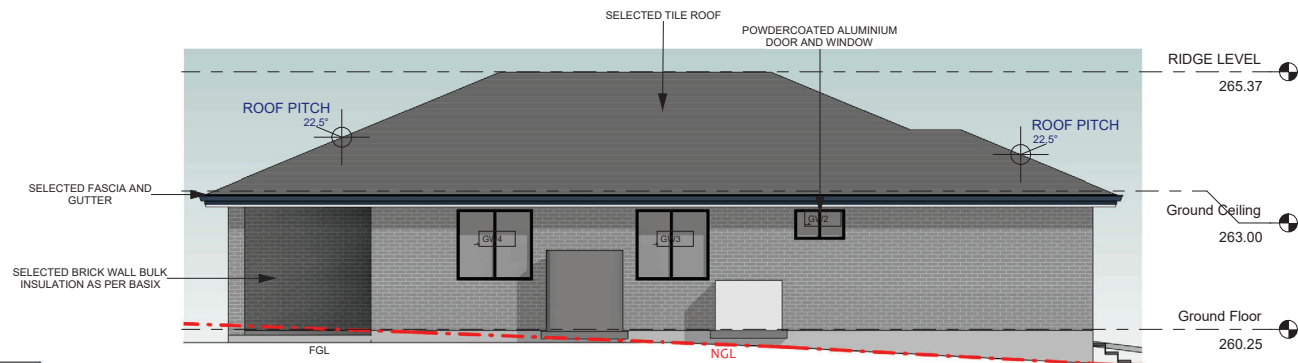

2 North-West Elevation
1 : 100



APPROVED PLAN
Development Consent:
DA/2026/415/1
Determined: 20/5/2026

REV	DATE	DESCRIPTION	BY
1	10-03-2026	DA ISSUE	

RUBY HOMES

THIS DRAWING IS THE EXCLUSIVE PROPERTY OF THE DEVELOPER & THE REPRODUCTION OF ANY PART WITHOUT THE PRIOR WRITTEN CONSENT OF THE DEVELOPER IS A VIOLATION OF APPLICABLE LAWS. IN NO EVENT SHALL THE DEVELOPER BE HELD LIABLE FOR SPECIAL, COLLATERAL, INCIDENTAL OR CONSEQUENTIAL LIABILITY IN CONNECTION WITH THE USE OF THIS DIGITAL DATA ONCE RELEASED FROM THE DEVELOPER'S OFFICE. THIS DRAWING IS TO BE READ & UNDERSTOOD IN CONJUNCTION WITH THE STRUCTURAL, MECHANICAL, ELECTRICAL & / OR ANY OTHER CONSULTANTS' DOCUMENTATION AS MAY BE APPLICABLE TO THE PROJECT PRIOR TO THE START OF ANY WORKS AND FOR ITS DURATION.

PROJECT:
LOT 38
13 KLENSENDORLFFE STREET
TAHMOOR


DRAWING TITLE:
ELEVATION 02

NORTH:


LOT NO:	DATE:	SCALE:	DRAWING No:	REV:
38	10-03-2026	1 : 100	DA.08	1
DRAWN BY:	CHECKED BY:	ISSUED BY:		
ROHIT	ROHIT	Nirja Aryal Silwal & Ram Prasad Silwal		

DA ISSUE

OnBuild Certifiers Pty Ltd
Reference: 260037
Date: 27/07/2026
Andrew Soliman
Director/ Principal Certifier
BDC2940
Consultant who prepared this document
remains responsible for accuracy

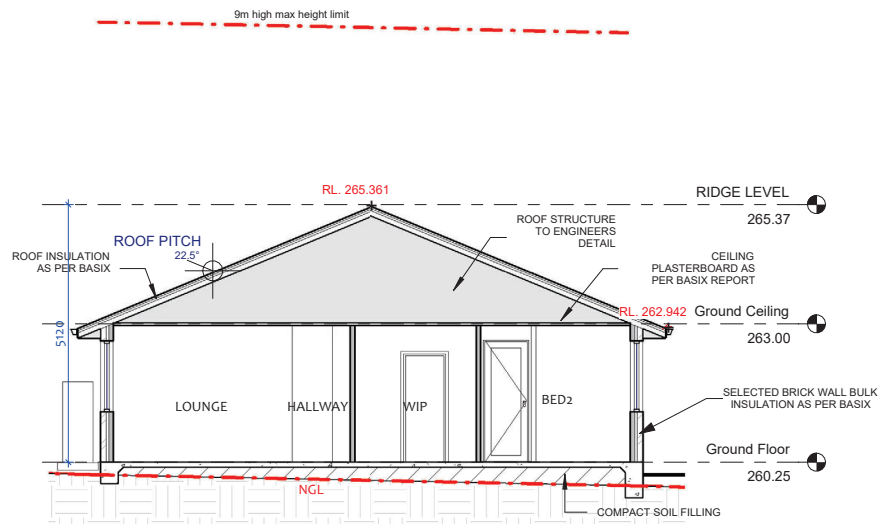

2 CROSS SECTION
1 : 100

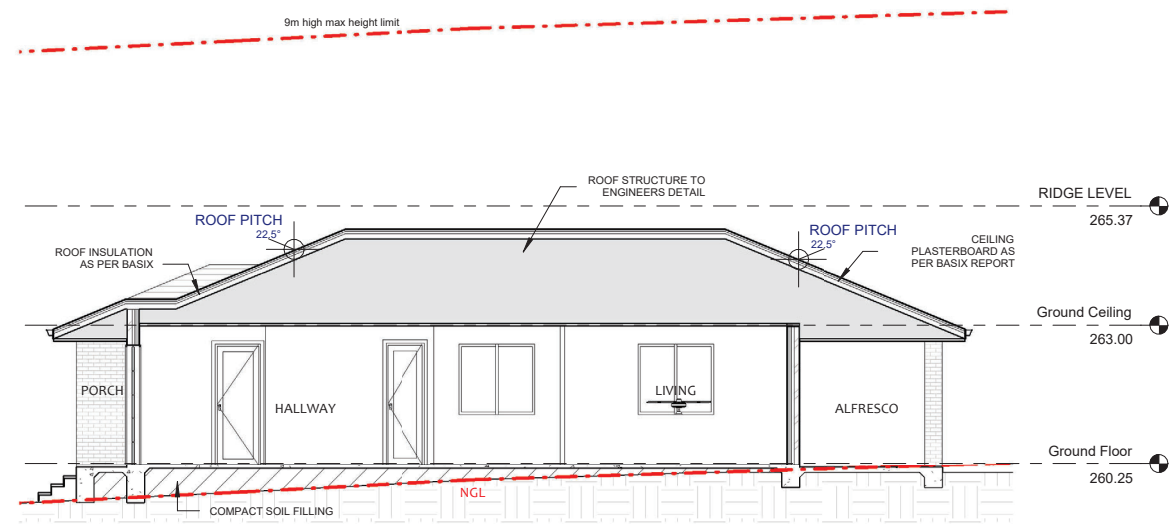

1 LONGITUDINAL SECTION
1 : 100



APPROVED PLAN
Development Consent:
DA/2026/415/1
Determined: 20/5/2026

REV	DATE	DESCRIPTION	BY
1	10-03-2026	DA ISSUE	



THIS DRAWING IS THE EXCLUSIVE PROPERTY OF THE DEVELOPER & THE REPRODUCTION OF ANY PART WITHOUT THE PRIOR WRITTEN CONSENT OF THE DEVELOPER IS A VIOLATION OF APPLICABLE LAWS. IN NO EVENT SHALL THE DEVELOPER BE HELD LIABLE FOR SPECIAL, COLLATERAL, INCIDENTAL OR CONSEQUENTIAL LIABILITY IN CONNECTION WITH THE USE OF THIS DIGITAL DATA ONCE RELEASED FROM THE DEVELOPER'S OFFICE. THIS DRAWING IS TO BE READ & UNDERSTOOD IN CONJUNCTION WITH THE STRUCTURAL, MECHANICAL, ELECTRICAL &/OR ANY OTHER CONSULTANT'S DOCUMENTATION AS MAY BE APPLICABLE TO THE PROJECT PRIOR TO THE START OF ANY WORKS AND FOR ITS DURATION.

PROJECT:
LOT 38

13 KLENSENDORLFFE STREET
TAHMOOR


DRAWING TITLE:
SECTIONS

NORTH:

LOT NO:	DATE:	SCALE:	DRAWING No:	REV:
38	10-03-2026	1 : 100	DA.09	1
DRAWN BY:	CHECKED BY:			ISSUED BY:
ROHIT	ROHIT			
CLIENT NAME: Nirja Aryal Silwal & Ram Prasad Silwal				

DA ISSUE

OnBuild Certifiers Pty Ltd
 Reference: 260037
 Date: 27/07/2026
 Andrew Soliman
 Director/ Principal Certifier
 BDC2940
 Consultant who prepared this document
 remains responsible for accuracy

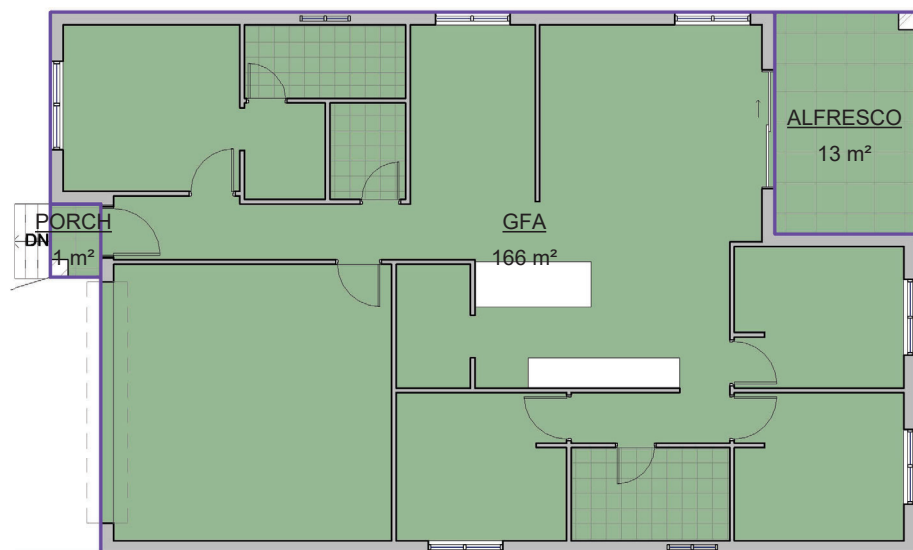

Area Schedule (Gross Building)	
Name	Area

Ground Floor	
GFA	166 m²
ALFRESCO	13 m²
PORCH	1 m²
Ground Floor: 3	180 m²
Grand total: 3	180 m²

1 Ground Floor
 1 : 100

REV	DATE	DESCRIPTION	BY
1	7-07-2026	Roof Changed to Colorbond - Ekta	

RUBY HOMES

THIS DRAWING IS THE EXCLUSIVE PROPERTY OF THE DEVELOPER & THE REPRODUCTION OF ANY PART WITHOUT THE PRIOR WRITTEN CONSENT OF THE DEVELOPER IS A VIOLATION OF APPLICABLE LAWS. IN NO EVENT SHALL THE DEVELOPER BE HELD LIABLE FOR SPECIAL, COLLATERAL, INCIDENTAL OR CONSEQUENTIAL LIABILITY IN CONNECTION WITH THE USE OF THIS DIGITAL DATA ONCE RELEASED FROM THE DEVELOPER'S OFFICE. THIS DRAWING IS TO BE READ & UNDERSTOOD IN CONJUNCTION WITH THE STRUCTURAL, MECHANICAL, ELECTRICAL & / OR ANY OTHER CONSULTANT'S DOCUMENTATION AS MAY BE APPLICABLE TO THE PROJECT PRIOR TO THE START OF ANY WORKS AND FOR ITS DURATION.

PROJECT:
LOT 38


13 KLENSENDORLFFE STREET
 TAHMOOR

DRAWING TITLE:
FLOOR AREA PLAN



CC ISSUE					
LOT NO: 38	DATE: 20-07-2026	SCALE: 1 : 100	DRAWING No: CC.10	REV: 1	ISSUED BY:
DRAWN BY: ROHIT	CHECKED BY: RH				
CLIENT NAME: Nirja Aryal Silwal & Ram Prasad Silwal					

OnBuild Certifiers Pty Ltd
Reference: 260037
Date: 27/07/2026
Andrew Soliman
Director/ Principal Certifier
BDC2940
Consultant who prepared this document
remains responsible for accuracy

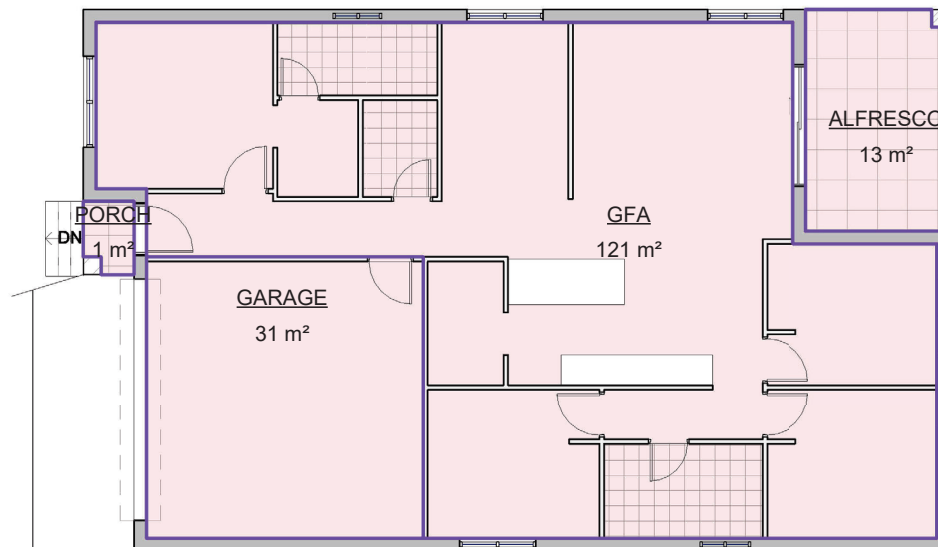

1 Ground Floor
1 : 100

Area Schedule (Rentable)	
Name	Area

Ground Floor	
GFA	121 m²
ALFRESCO	13 m²
GARAGE	31 m²
PORCH	1 m²
Ground Floor: 4	166 m²
Grand total: 4	166 m²

1	7-07-2026	Roof Changed to Colorbond - Ekta	BY
REV	DATE	DESCRIPTION	BY

RUBY HOMES

THIS DRAWING IS THE EXCLUSIVE PROPERTY OF THE DEVELOPER & THE REPRODUCTION OF ANY PART WITHOUT THE PRIOR WRITTEN CONSENT OF THE DEVELOPER IS A VIOLATION OF APPLICABLE LAWS. IN NO EVENT SHALL THE DEVELOPER BE HELD LIABLE FOR SPECIAL, COLLATERAL, INCIDENTAL OR CONSEQUENTIAL LIABILITY IN CONNECTION WITH THE USE OF THIS DIGITAL DATA ONCE RELEASED FROM THE DEVELOPER'S OFFICE. THIS DRAWING IS TO BE READ & UNDERSTOOD IN CONJUNCTION WITH THE STRUCTURAL, MECHANICAL, ELECTRICAL & / OR ANY OTHER CONSULTANT'S DOCUMENTATION AS MAY BE APPLICABLE TO THE PROJECT PRIOR TO THE START OF ANY WORKS AND FOR ITS DURATION.

PROJECT:
LOT 38
13 KLENSENDORLFFE STREET
TAHMOOR

DRAWING TITLE:
RENTABLE AREA PLAN



LOT NO: 38	DATE: 20-07-2026	SCALE: 1 : 100	DRAWING No: CC.11	REV: 1
DRAWN BY: ROHIT	CHECKED BY: RH			ISSUED BY:
CLIENT NAME: Nirja Aryal Silwal & Ram Prasad Silwal				

CC ISSUE

OnBuild Certifiers Pty Ltd
Reference: 260037
Date: 27/07/2026
Andrew Soliman
Director/ Principal Certifier
BDC2940
Consultant who prepared this document
remains responsible for accuracy



	1. RF	2. BR1	3. AL	4. ED	5. GD	6. FAS	7. GUT
	ROOF	MAIN WALLS	WINDOWS/ BALUSTRADE	MAIN DOOR	GARAGE DOOR	FASCIA	GUTTER
MATERIAL	Concrete TILE finish shale grey	SELECTED AUSTRAL OR PPH BRICK FROM BUILDER RANGE	Manufacturer: ABM Door & Window Finish: Monument	TIMBER	COLORBOND Finish dover white or similar	Manufacturer: Colorbond® Finish : Monument	Manufacturer: Colorbond® Finish : Monument
COLOUR							

NOTE : ALL COLOURS SPECIFIED ARE INDICATIVE ONLY AND ARE SUBJECT TO VARIATION AND TO AVAILABILITY
ANY DISCREPANCY PLEASE FOLLOW AS PER RENDERED IMAGE



NOTE : ALL COLOURS SPECIFIED ARE INDICATIVE ONLY AND ARE SUBJECT TO VARIATION AND TO AVAILABILITY
ANY DISCREPANCY PLEASE FOLLOW AS PER RENDERED IMAGE


REV	DATE	DESCRIPTION	BY
1	10-03-2026	DA ISSUE	

RUBY HOMES

THIS DRAWING IS THE EXCLUSIVE PROPERTY OF THE DEVELOPER & THE REPRODUCTION OF ANY PART WITHOUT THE PRIOR WRITTEN CONSENT OF THE DEVELOPER IS A VIOLATION OF APPLICABLE LAWS. IN NO EVENT SHALL THE DEVELOPER BE HELD LIABLE FOR SPECIAL COLLATERAL, INCIDENTAL OR CONSEQUENTIAL LIABILITY IN CONNECTION WITH THE USE OF THIS DIGITAL DATA ONCE RELEASED FROM THE DEVELOPER'S OFFICE. THIS DRAWING IS TO BE READ & UNDERSTOOD IN CONJUNCTION WITH THE STRUCTURAL, MECHANICAL, ELECTRICAL & / OR ANY OTHER CONSULTANT'S DOCUMENTATION AS MAY BE APPLICABLE TO THE PROJECT PRIOR TO THE START OF ANY WORKS AND FOR ITS DURATION.

PROJECT: LOT 38	DRAWING TITLE: COLOR SCHEDULE	NORTH:	LOT NO: 38	DATE: 10-03-2026	SCALE: 1 : 100	DRAWING No: DA.12	REV: 1
13 KLENSENDORLFFE STREET TAHMOOR			DRAWN BY: ROHIT	CHECKED BY: ROHIT			ISSUED BY:
			CLIENT NAME: Nirja Aryal Silwal & Ram Prasad Silwal				

KLENSENDORLFFE STREET

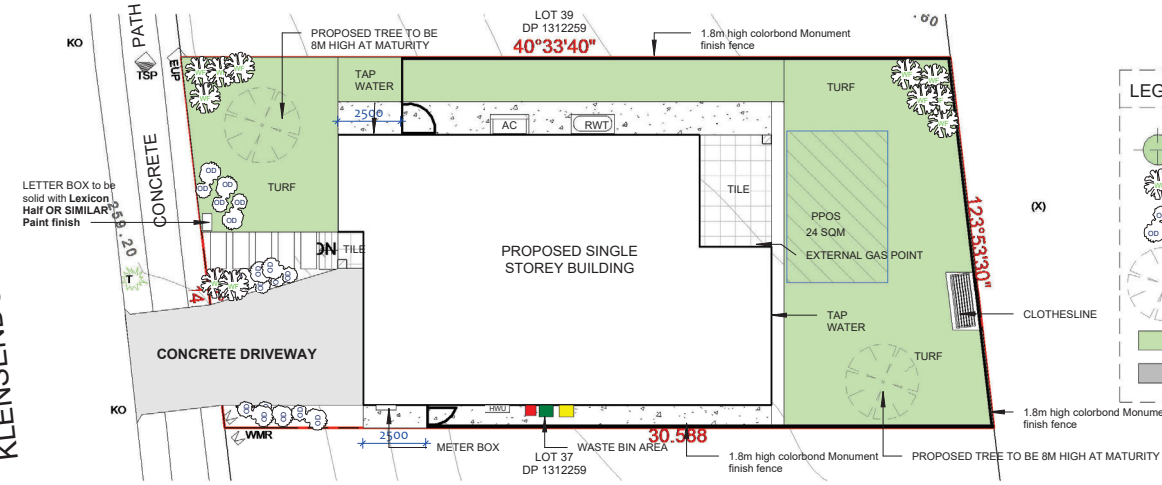

DA - LANDSCAPE PLAN

1 : 200

GENERAL NOTES:

- LANDSCAPE CONTRACTOR TO CHECK DA CONDITIONS AND STAMPED LANDSCAPE PLAN.
- BEFORE COMMENCING WORKS TO ENSURE NO ADDITIONS/AMENDMENTS TO PLAN.
- GARDEN BEDS IN OSD BASIN TO CONSIST OF NON FLOATABLE DECORATIVE GRAVEL.
- REFER TO HYDRAULICS ENGINEERS PLAN FOR OSD DETAILS/FINAL LEVELS.
- MULCHED PLANTING BEDS TO BE A MINIMUM DEPTH OF 75mm AS SELECTED.
- CONTRACTOR'S RESPONSIBILITY TO CHECK AND ADJUST SOIL pH AS REQUIRED.
- PROVIDE TIMBER EDGE AS A MINIMUM BENEATH FENCING/GATES TO DEFINE TURF AND GARDEN BEDS/PATHWAYS. EDGING TO BE PROVIDED TO ALL AREAS WHERE DIFFERING MATERIALS MEET i.e TURF/GARDEN, TURF/GRAVEL PATH ETC.
- WEED MAT BENEATH GRAVEL PATHWAYS REQUIRED TO LIMIT MUD TRACKING.
- PREMIUM ORGANIC GARDEN MIX TO BE USED.
- ALL PLANTS TO BE HEALTHY AND VIGOROUS.
- CONTRACTOR TO MAKE GOOD TURF ON NATURE STRIP POST CONSTRUCTION.
- CONTRACTOR TO MAKE GOOD TURF ON NATURE STRIP POST CONSTRUCTION.
- DO NOT SCALE ARCHITECTURAL SETOUT FROM LANDSCAPE DRAWING.
- EXISTING TREE SPREAD APPROXIMATE ONLY. REFER TO TREE REPORT WHEN APPLICABLE.
- SITE SURVEY PROVIDED BY OTHERS.
- BUFFALO TURF PREFERRED OVER KIKUYU.

LANDSCAPE BASIX NOTE:

THE APPLICANT MUST PLANT INDIGENEOUS OR LOW WATER USE SPECIES OF VEGETATION THROUGHOUT 15 SQM OF THE SITE.

NOTE: BUILDER RESERVES THE RIGHT NOT TO UNDERTAKE NOR SUPPLY CERTIFICATE FOR OCCUPATION CERTIFICATE.

NOTE: TO AID COMPLIANCE WITH BASIX LEGISLATION, PLANTS (WHERE APPLICABLE) HAVE BEEN SELECTED FROM THE LOCAL CITY COUNCIL SHIRE PLANT LISTS.

NOTE: LOCATION OF SEWER MAINS LINES, WATER PIPES, UNDERGROUND ELECTRICITY AND OTHER SERVICES MUST BE OBTAINED PRIOR TO COMMENCEMENT OF ANY WORK ON SITE.

CONTRACTORS NOTE: CALCULATED AREAS DETERMINED BY CAD AND HAVE BEEN ROUNDED UP FOR USE AS A GUIDE ONLY. ALLOW STANDARD PERCENTAGE FOR CUTTING AND WASTAGE. CONFIRM DIMENSIONS AND NUMBERS PRIOR TO QUOTING/ORDERING.

REAR LANDSCAPE area = 120.0m²
FRONT LANDSCAPE AREA = 55.0m²
TOTAL LANDSCAPE AREA = 175.0m²





PLANT SCHEDULE

Genus	Common Name	Qty	Pot size	Height	width
Trees					
Backhousia myrtifolia	Grey Myrtle	1	45L	6-10m	Dense feature tree with, green glossy foliage. Greenish yellow flowers in small terminal clusters.
Shrubs					
Bursaria Spinosa Var Sppinosa	Blackthorn, Boxthorn	8	140mm	1.5m	Thorny, wiry branches. Leaf size and shape varies with age. Small, white fragrant flowers.
Dodonea Visco ssp. Cuneata	Wedge-Leaft Hop Bush	6	140mm	1m	Compact growth. Sticky leaves taper to sharp point. Green fruit turns red and purple.
Indigofera Australis	Native Indigo	5	140mm	1m	Slender, erect. Pink to lilac pea flowers, numerous along stems.
Hedging & screening Plants					
Acmena smithii 'Cherry Surprise'	Lilly Pilly Cherry Surprise PBR	10	140mm	3m	It has attractive small dense green foliage that provides a continuous flush of cherry-red new growth nearly all year round. Small white starry flowers bloom in summer.



OnBuild Certifiers Pty Ltd
Reference: 260037
Date: 27/07/2026
Andrew Soliman
Director/ Principal/Certifier
BDC2940

Consultant who prepared this document remains responsible for accuracy

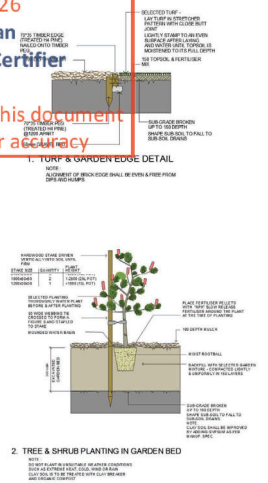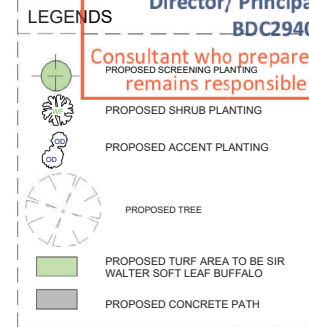

DA ISSUE

REV	DATE	DA ISSUE	DESCRIPTION	BY
1	10-03-2026	DA ISSUE		



PROJECT:
LOT 38

13 KLENSENDORLFFE STREET
TAHMOOR

DRAWING TITLE:
LANDSCAPE PLAN



LOT NO: 38	DATE: 10-03-2026	SCALE: 1 : 200	DRAWING No: DA.13	REV: 1
DRAWN BY: ROHIT	CHECKED BY: ROHIT			ISSUED BY:
CLIENT NAME: Nirja Aryal Silwal & Ram Prasad Silwal				

ABCB HOUSING PROVISIONS : PART 10.2 WET AREA WATERPROOFING

10.2.1 Wet Areas

- Building elements in wet areas within a building must be protected with a waterproofing system.
- The waterproofing system in (1) must be either waterproof or water resistant in accordance with 10.2.2 to 10.2.6.

10.2.2 Shower Area (enclosed and unenclosed)

- For a shower area with a hob, step-down or level threshold, the following applies:
 - The floor of the shower area must be waterproof, including any hob or step-down (see Figure 10.2.2); and
 - The walls of the shower area must be waterproof not less than 1800 mm above the floor substrate (see Figure 10.2.2).
 - Wall junctions and joints within the shower area must be waterproof not less than 40 mm either side of the junction (see Figure 10.2.2).
 - Wall/floor junctions within the shower area must be waterproof (see Figure 10.2.2).
 - Penetrations within the shower area must be waterproof.
- A shower with a preformed shower base must also comply with the requirements of (1), except for (a) which is not applicable.

Figure 10.2.2: Extent of treatment for shower areas - concrete compressed fibre-cement and fibre-cement sheet floors.

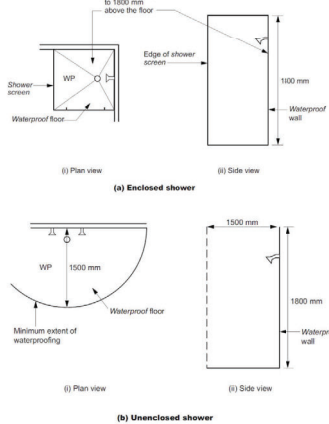


Figure Notes
Wall/floor junction heights are to be as per 10.2.2 to 10.2.6 (as applicable).

Notes
Where a shower is above a bath or spa, use requirements for shower.

10.2.3 Area outside shower area

- For concrete, compressed fibre-cement and fibre-cement sheet flooring, the floor of the room must be water resistant.
- For timber floors including particleboard, plywood and other timber based flooring materials, the floor of the room must be waterproof.
- Wall/floor junctions must be -
 - waterproof, and
 - where a flashing is used, the horizontal leg must be not less than 40 mm.

10.2.4 Areas adjacent to baths and spas without showers

- For areas adjacent to all baths and spas, the following applies:
 - For concrete, compressed fibre-cement and fibre-cement sheet flooring, the floor of the room must be water resistant.
 - For timber floors including particleboard, plywood and other timber based flooring materials, the floor of the room must be waterproof.
 - Tap and spout penetrations must be waterproof where they occur in horizontal surfaces.
- For areas adjacent to non-freestanding baths and spas, the following applies:
 - Walls must be water resistant (see Figure 10.2.4a and Figure 10.2.4b).
 - to a height of not less than 150mm above the vessel, for the extent of the vessel, where the vessel is within 75mm of a wall and
 - for all exposed surfaces below vessel lip.
 - Wall junctions and joints must be water resistant within 150mm above a vessel for the extent of the vessel.
 - Wall/floor junctions must be waterproof for the extent of the vessel (see Figure 10.2.4a and Figure 10.2.4b).
- For inserted baths and spas, the following applies:
 - For floors and horizontal surfaces:
 - Any shelf area adjoining the bath or spa must be waterproof and include a waterstop under the vessel lip.
 - There are no requirements for the floor under a bath or spa.
 - For walls:
 - Waterproof to not less than 150mm above the lip of a bath or spa.
 - There are no requirements for the floor under a bath or spa.
 - For wall junctions and joints, the following applies:
 - Waterproof junctions within 150mm of a bath or spa.
 - There are no requirements for junctions and joints in walls beneath the lip of a bath or spa.
 - Tap and spout penetrations must be waterproof where they occur in horizontal surfaces.

Figure 10.2.4a: Areas adjacent to baths and spas without showers for concrete, compressed fibre-cement and fibre-cement sheet flooring




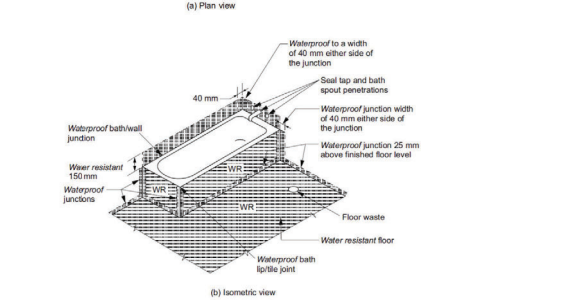



Figure 10.2.4b: Areas adjacent to baths and spas without showers for timber floors including particle-board, plywood and other floor materials

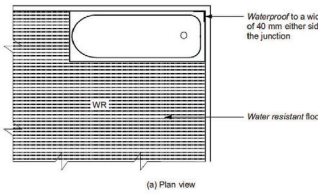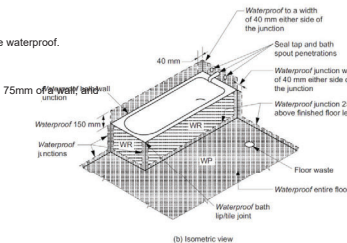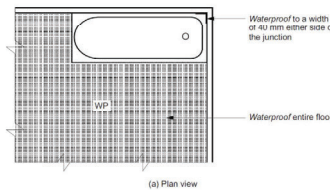

10.2.5 Other areas

- For walls adjoining other types of vessels (not sink, bath or tub) (b), the following applies:
 - Walls must be water resistant to a height of not less than 150mm above the vessel, for the extent of the vessel, where the vessel is within 75 mm of a wall (see Figure 10.2.5).
 - Waterproof wall.
 - Waterproof tap and spout penetrations where they occur in surfaces required to be waterproof or water resistant.
- For laundries and WCs, the following applies:
 - The floor of the room must be water resistant.
 - Wall/floor junctions must be water resistant and where a flashing is used, the horizontal leg must be not less than 40 mm.
- For WCs with a handheld bidet spray installation, the following applies:
 - The floor of the room must be waterproof.
 - Walls must be -
 - waterproof in WC area within a 900 mm radius from the wall connection of the handheld bidet spray device to a height of not less than 150mm above the floor substrate; and
 - water resistant in WC area within a 900 mm radius from the wall connection of the handheld bidet device to not less than 1200 mm above the finished floor level of the WC.
 - Wall junctions within the WC area within 900 mm radius from the wall connection of the handheld bidet spray device must be waterproof.
 - Wall/floor junctions within the WC area within 1000 mm radius from the wall connection of the handheld bidet spray device must be waterproof.
 - Penetrations in the WC area must be waterproof.

Figure 10.2.5: Bath and vessel abutting wall - areas to be protected

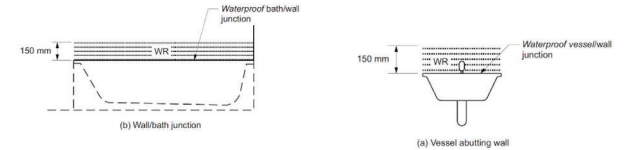

10.2.6 Waterproofing systems

- For the purposes of this Part, a waterproofing system is deemed -
 - waterproof, if it complies with (2); or
 - water resistant, if it complies with (3).
- For a waterproofing system required to be waterproof in accordance with 10.2.2 to 10.2.5, the materials nominated in 10.2.8 must be used.
- For a waterproofing system required to be water resistant in accordance with 10.2.2 to 10.2.5, the materials nominated in 10.2.9 must be used in conjunction with the materials in 10.2.10.

10.2.12 Construction of wet area floors - falls

- Where a floor waste is installed -
- the minimum continuous fall of a floor plane to the waste must be 1:80; and
 - the maximum continuous fall of a floor plane to the waste must be 1:50.

OnBuild Certifiers Pty Ltd
Reference: 260037
Date: 27/07/2026

Noted this document is responsible for accuracy
Director, Principal Certifier
BDC2940

REV	DATE	DESCRIPTION	BY



RUBY HOMES

THIS DRAWING IS THE EXCLUSIVE PROPERTY OF THE DEVELOPER & THE REPRODUCTION OF ANY PART WITHOUT THE PRIOR WRITTEN CONSENT OF THE DEVELOPER IS A VIOLATION OF APPLICABLE LAWS. IN NO EVENT SHALL THE DEVELOPER BE HELD LIABLE FOR SPECIAL, COLLATERAL, INCIDENTAL OR CONSEQUENTIAL LIABILITY IN CONNECTION WITH THE USE OF THIS DIGITAL DATA ONCE RELEASED FROM THE DEVELOPER'S OFFICE. THIS DRAWING IS TO BE READ & UNDERSTOOD IN CONJUNCTION WITH THE STRUCTURAL, MECHANICAL, ELECTRICAL & / OR ANY OTHER CONSULTANT'S DOCUMENTATION AS MAY BE APPLICABLE TO THE PROJECT PRIOR TO THE START OF ANY WORKS AND FOR ITS DURATION.

PROJECT:
LOT 38

13 KLENSENDORLFFE STREET
TAHMOOR

DRAWING TITLE:
**WATERPROOFING
DETAILS**

NORTH:

LOT NO:	DATE:	SCALE:	DRAWING No:	REV:
38	20-07-2026	1 : 50	CC.16	
DRAWN BY:	CHECKED BY:	ISSUED BY:		
ROHIT	RH	Nirja Aryal Silwal & Ram Prasad Silwal		

This certificate confirms that the proposed development will meet the NSW government's requirements for sustainability. If it is built in accordance with the requirements set out below, Terms and Conditions apply to the development. Please have the meaning given by the Document entitled "BASIX Certificate" dated 10/06/2020 published by the Department. This document is available at: www.planningportal.nsw.gov.au/developments

Secretary
Date of issue: Monday, 19 March 2020
To be valid, this certificate must be submitted with a development application or lodged with a planning development certificate application when it provides the site of the site.



Project summary			
Project name	13 KLENSENDORLFFE STREET		
Street address	13 KLENSENDORLFFE STREET TAHMOOR (201)		
Local Government area	Woolondilly Shire Council		
Plan type and plan number	Deceased Plan (DP112229)		
Lot no.	3		
Section no.			
Project type	single house (detached)		
No. of bedrooms	4		
Project score			
Score	17	Target 45	
Thermal Performance			
Thermal Performance	Pass	Target Pass	
Energy			
Energy	71	Target 70	
Materials			
Materials	19	Target 19	

Certificate Prepared by	
Name / Company Name	HOMEDALE PTY LTD
ABN (if applicable)	760376156

Description of project

Project address		Assessor details and thermal loads	
Project name	13 KLENSENDORLFFE STREET	Assessor's assessment number	NS
Street address	13 KLENSENDORLFFE STREET TAHMOOR	NHRSRS certificate number	NS
Local Government area	Woolondilly Shire Council	Climate zone	NS
Plan type and plan number	Deceased Plan (DP112229)	Area of existing building (m ²)	NS
Lot no.	3	Area of existing building (m ²)	NS
Section no.		Area of existing building (m ²)	NS
Project score			
Score	17	Target 45	
Thermal Performance			
Thermal Performance	Pass	Target Pass	
Energy			
Energy	71	Target 70	
Materials			
Materials	19	Target 19	

Schedule of BASIX commitments

The commitments set out below regulate how the proposed development is to be carried out. It is a condition of any development consent granted, or complying development certificate issued, for the proposed development, that BASIX commitments be complied with.

Water Commitments			
Shower on 24 plans	Shower on CCDC plans & spaces	Comply	Check
The applicant must install showerheads with a minimum rating of 4 star (4.5 bar) or 6 L/min plus spray force and/or coverage limits in all showers in the development.			
The applicant must install a low-flow showering system with a minimum rating of 4 star in each toilet in the development.			
The applicant must install taps with a minimum rating of 4 star in the kitchen in the development.			
The applicant must install basin taps with a minimum rating of 4 star in each bathroom in the development.			
Alternative water			
The applicant must install a rainwater tank of at least 5000 litres on the site. This rainwater tank must meet, and be installed in accordance with, the requirements of AS 4793, including any relevant standards.			
The applicant must configure the rainwater tank to collect rain runoff from at least 223 square metres of the roof area of the development (excluding the area of the roof that drains to any intermediate tank or private dam).			
The applicant must connect the rainwater tank to:			
• the cold water tap that supplies each outdoor shower in the development			
• the cold water tap that supplies each outdoor toilet in the development			
• the cold water tap that supplies each outdoor shower in the development			

Thermal Performance and Materials commitments			
Shower on 24 plans	Shower on CCDC plans & spaces	Comply	Check
The applicant must install the rainwater tank to collect rain runoff from at least 223 square metres of the roof area of the development (excluding the area of the roof that drains to any intermediate tank or private dam).			
The applicant must connect the rainwater tank to:			
• the cold water tap that supplies each outdoor shower in the development			
• the cold water tap that supplies each outdoor toilet in the development			
• the cold water tap that supplies each outdoor shower in the development			

Energy Commitments			
Shower on 24 plans	Shower on CCDC plans & spaces	Comply	Check
The applicant must install the rainwater tank to collect rain runoff from at least 223 square metres of the roof area of the development (excluding the area of the roof that drains to any intermediate tank or private dam).			
The applicant must connect the rainwater tank to:			
• the cold water tap that supplies each outdoor shower in the development			
• the cold water tap that supplies each outdoor toilet in the development			
• the cold water tap that supplies each outdoor shower in the development			

OnBuild Certifiers Pty Ltd
Reference: 260037
Date: 27/07/2026
Andrew Soliman
Director/ Principal Certifier
BDC2940
Consultant who prepared this document
remains responsible for accuracy

Legend	
In these commitments, "applicant" means the person carrying out the development.	
Commitments identified with a "W" in the "Shower on 24 plans" column must be shown on the plans accompanying the development application for the proposed development (if a development application is to be lodged for the proposed development).	
Commitments identified with a "W" in the "Shower on CCDC plans & spaces" column must be shown in the plans and specifications accompanying the application for a construction certificate (if a construction certificate is to be lodged for the proposed development).	
Commitments identified with a "W" in the "Comply" column must be certified by a certifying authority as having been fulfilled, before a final occupation certificate (either interim or final) for the development may be issued.	

APPROVED PLAN
Development Consent:
DA/2026/415/1
Determined: 20/5/2026
Wollondilly Shire Council

						PROJECT: LOT 38		DRAWING TITLE: BASIX		NORTH: 		LOT NO: 38		DATE: 10-03-2026		SCALE:		DRAWING No: CC.16		REV: 1	
				THIS DRAWING IS THE EXCLUSIVE PROPERTY OF THE DEVELOPER & THE REPRODUCTION OF ANY PART WITHOUT THE PRIOR WRITTEN CONSENT OF THE DEVELOPER IS A VIOLATION OF APPLICABLE LAWS. IN NO EVENT SHALL THE DEVELOPER BE HELD LIABLE FOR SPECIAL, COLLATERAL, INCIDENTAL OR CONSEQUENTIAL LIABILITY IN CONNECTION WITH THE USE OF THIS DIGITAL DATA ONCE RELEASED FROM THE DEVELOPER'S OFFICE. THIS DRAWING IS TO BE READ & UNDERSTOOD IN CONJUNCTION WITH THE STRUCTURAL, MECHANICAL, ELECTRICAL & OR ANY OTHER CONSULTANTS' DOCUMENTATION AS MAY BE APPLICABLE TO THE PROJECT PRIOR TO THE START OF ANY WORKS AND FOR ITS DURATION.		13 KLENSENDORLFFE STREET TAHMOOR						DRAWN BY: ROHIT		CHECKED BY: ROHIT				ISSUED BY:			
												CLIENT NAME:									

REV	DATE	DA ISSUE	DESCRIPTION	BY
1	10-03-2026	DA ISSUE		

RUBY HOMES
THIS DRAWING IS THE EXCLUSIVE PROPERTY OF THE DEVELOPER & THE REPRODUCTION OF ANY PART WITHOUT THE PRIOR WRITTEN CONSENT OF THE DEVELOPER IS A VIOLATION OF APPLICABLE LAWS. IN NO EVENT SHALL THE DEVELOPER BE HELD LIABLE FOR SPECIAL, COLLATERAL, INCIDENTAL OR CONSEQUENTIAL LIABILITY IN CONNECTION WITH THE USE OF THIS DIGITAL DATA ONCE RELEASED FROM THE DEVELOPERS OFFICE. THIS DRAWING IS TO BE READ & UNDERSTOOD IN CONJUNCTION WITH THE STRUCTURAL, MECHANICAL, ELECTRICAL &/OR ANY OTHER CONSULTANT'S DOCUMENTATION AS MAY BE APPLICABLE TO THE PROJECT PRIOR TO THE START OF ANY WORKS AND FOR ITS DURATION.

PROJECT:
LOT 38
13 KLENSENDORLFFE STREET
TAHMOOR

DRAWING TITLE:
BASIX



NORTH:
LOT NO:
38
DATE:
10-03-2026
SCALE:
DRAWING No:
CC.16
REV:
1
ISSUED BY:
Nirja Aryal Silwal & Ram Prasad Silwal