
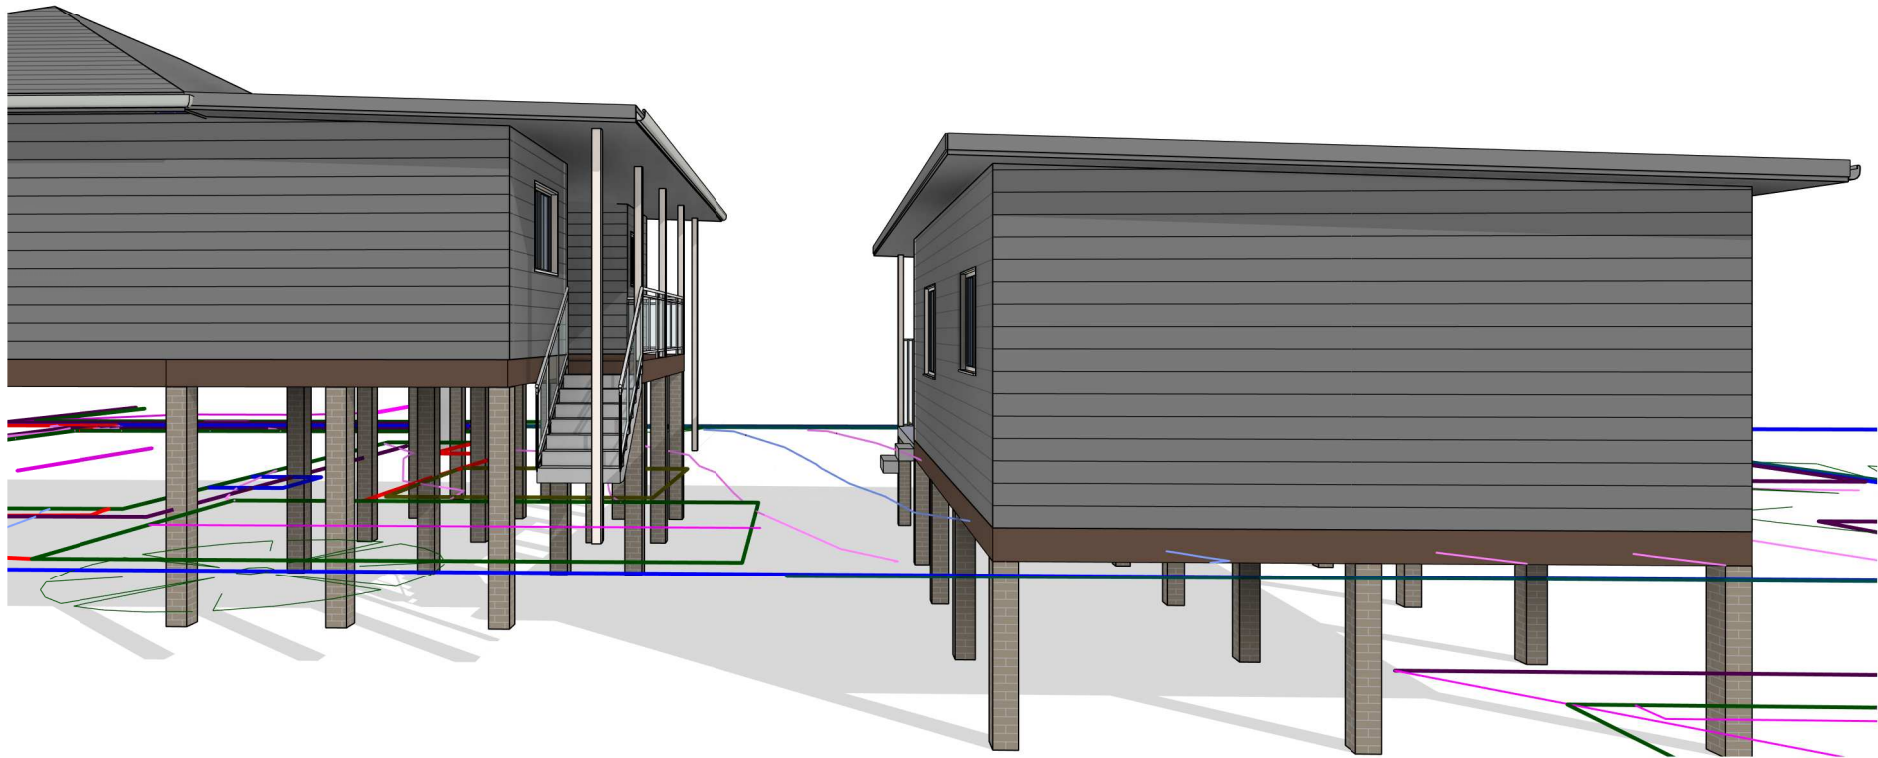


DEMOLITION OF EXISTING AWNING & GARAGE &
PROPOSED SECONDARY DWELLING
AND NEW ADDITIONS TO EXIST. HOUSE
AT: NO.6 BELLEVUE STREET, BLACKTOWN, NSW 2148

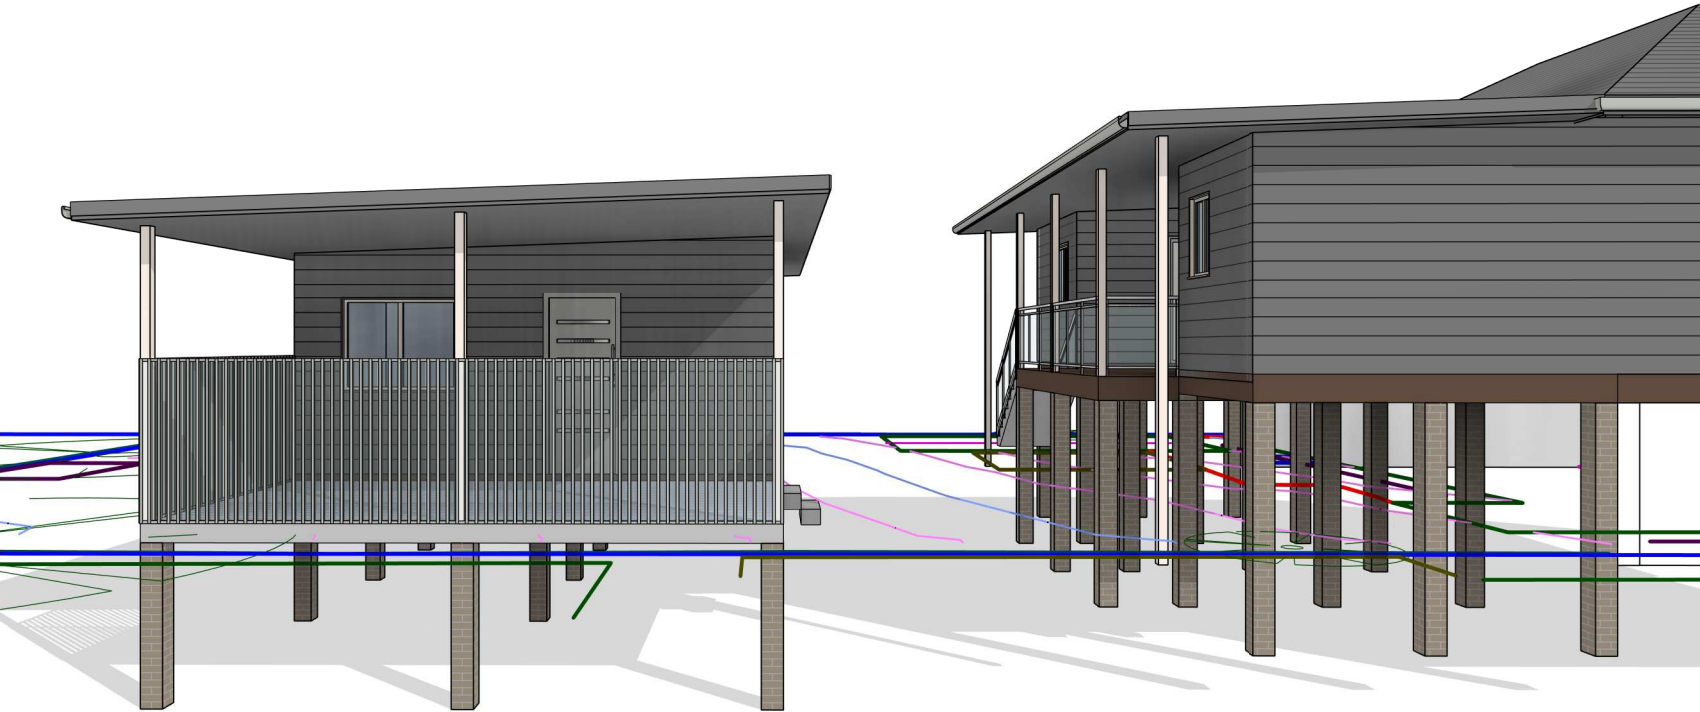

SHEET LIST	
SHEET NUMBER	SHEET NAME
GF-0126-00	3D VIEWS
GF-0126-01	SITE/ROOF PLAN
GF-0126-02	EXISTING AND DEMOLITION PLAN
GF-0126-03	PROPOSED GROUND FLOOR PLAN
GF-0126-04	ELEVATIONS
GF-0126-05	ELEVATIONS (ADDITONS)
GF-0126-06	SECTIONS
GF-0126-07	EROSION & SEDIMENT CONTROL PLAN
GF-0126-08	BASIX COMMITMENTS PLAN
GF-0126-09	BASIX COMMITMENTS
GF-0126-10	WET AREAS PLAN
GF-0126-11	TYPICAL WATERPROOFING CONSTRUCTION DETAILS

© THIS DRAWING IS THE PROPERTY OF LT DESIGN & CONSULTING PTY LTD AND WE RESERVE THE COPYRIGHT TO ALL OUR DESIGNS WHICH CANNOT BE REPRODUCED (IN PART OR IN WHOLE) BEFORE FIRST OBTAINING WRITTEN CONSENT. CONTRAVENTION WILL BE PROSECUTED

• FIGURED DIMENSIONS TO BE TAKEN IN PREFERENCE TO SCALE.

• BUILDERS' WORK TO COMPLY WITH THE LATEST BCA AND ITS AMENDMENTS AND RELEVANT AUSTRALIAN STANDARDS REFERRED WITHIN.

No.	Description	Date



Building Design | 3D Modeling | Drafting | Detailing



Accreditation No: 6302
Shop 6A/80 Thorney Rd, Fairfield West
0414 891 998 - Le@LTDesign.net.au

BUILDING
DESIGNERS
AUSTRALIA

DRAWING:
3D VIEWS

CLIENT & PROJECT: LOT 152 IN DP 28393
DEMOLITION OF EXISTING AWNING & GARAGE & PROPOSED
SECONDARY DWELLING AND NEW ADDITIONS TO EXIST. HOUSE
AT: NO.6 BELLEVUE STREET, BLACKTOWN

COMPLYING DEVELOPMENT CERTIFICATE

DATE:
16/04/2026
DWG NO:
GF-0126-00

SCALE:



DRW BY:
LT
(A3)

SITE CALCULATIONS - SEPP 2021				
SITE AREA: 587.4 SQM	EXISTING	PROPOSED	REQUIRED	COMPLY
EXISTING GROUND FLOOR	86.75 sqm			
EXISTING SHEDS	13.5 sqm			
PROPOSED ADDITIONS		20.5 sqm		
PROPOSED SECONDARY DWELLING		60 sqm	60 sqm (Max.)	YES
TOTAL FLOOR AREA	180.75 sqm		330 sqm (Max.)	YES
PRIVATE OPEN SPACE	24.1 sqm		MORE THAN 24 SQM	YES
LANDSCAPE AREA	190.58 sqm (32.44%)		20% (Min.)	YES
SITE COVERAGE	219 sqm (37.28%)		50% (Max.)	YES

NOTES:

1. CHECK DIMENSIONS ON SITE BEFORE PROCEEDING WITH THE WORK OF THE CONTRACT. NOTIFY BUILDING DESIGNER OF OMISSIONS OR CONFLICT IN DRAWINGS OR SPECIFICATIONS.
2. FIGURED DIMENSIONS ARE TO BE TAKEN IN PREFERENCE TO SCALE. DO NOT SCALE OFF DRAWINGS.
3. ALL CONSTRUCTION WORK IS TO COMPLY WITH RELEVANT AUSTRALIAN STANDARDS AND THE NCC.
4. REFER TO ACCOMPANYING BASIX CERTIFICATE REFERENCED FOR COMMITMENTS FOR THIS DEVELOPMENT.
5. **SA:** SMOKE ALARM
SMOKE ALARMS TO BE INSTALLED IN ACCORDANCE WITH AS 3786-2014 & CONNECTED TO MAINS POWER

WINDOW SCHEDULE		
Mark	Width	Height
W1	1200	1000
W2	1500	1200
W3	1500	1200
W4	1500	1200
W5	600	900


ADDITIONS		
Mark	Width	Height
W1'	600	900
W2'	1200	1000

SITE CALCULATIONS - SEPP 2008				
SITE AREA: 587.4 SQM	EXISTING	PROPOSED	REQUIRED	COMPLY
EXISTING GROUND FLOOR	81.42 sqm			
EXISTING SHEDS	13.5 sqm			
PROPOSED ADDITIONS		16.9 sqm		
PROPOSED SECONDARY DWELLING		54 sqm		
TOTAL FLOOR AREA	165.82 sqm		296.85 sqm (Max.)	YES
PRIVATE OPEN SPACE	24.1 sqm		MIN. 24 SQM	YES
LANDSCAPE AREA	190.58 sqm (32.44%)		20% (Min.)	YES

LOT 152 - DP 28393

DEMOLITION OF EXISTING AWNING & GARAGE & PROPOSED SECONDARY DWELLING AND NEW ADDITIONS TO EXIST. HOUSE

AT: NO.6 BELLEVUE STREET, BLACKTOWN, NSW 2148

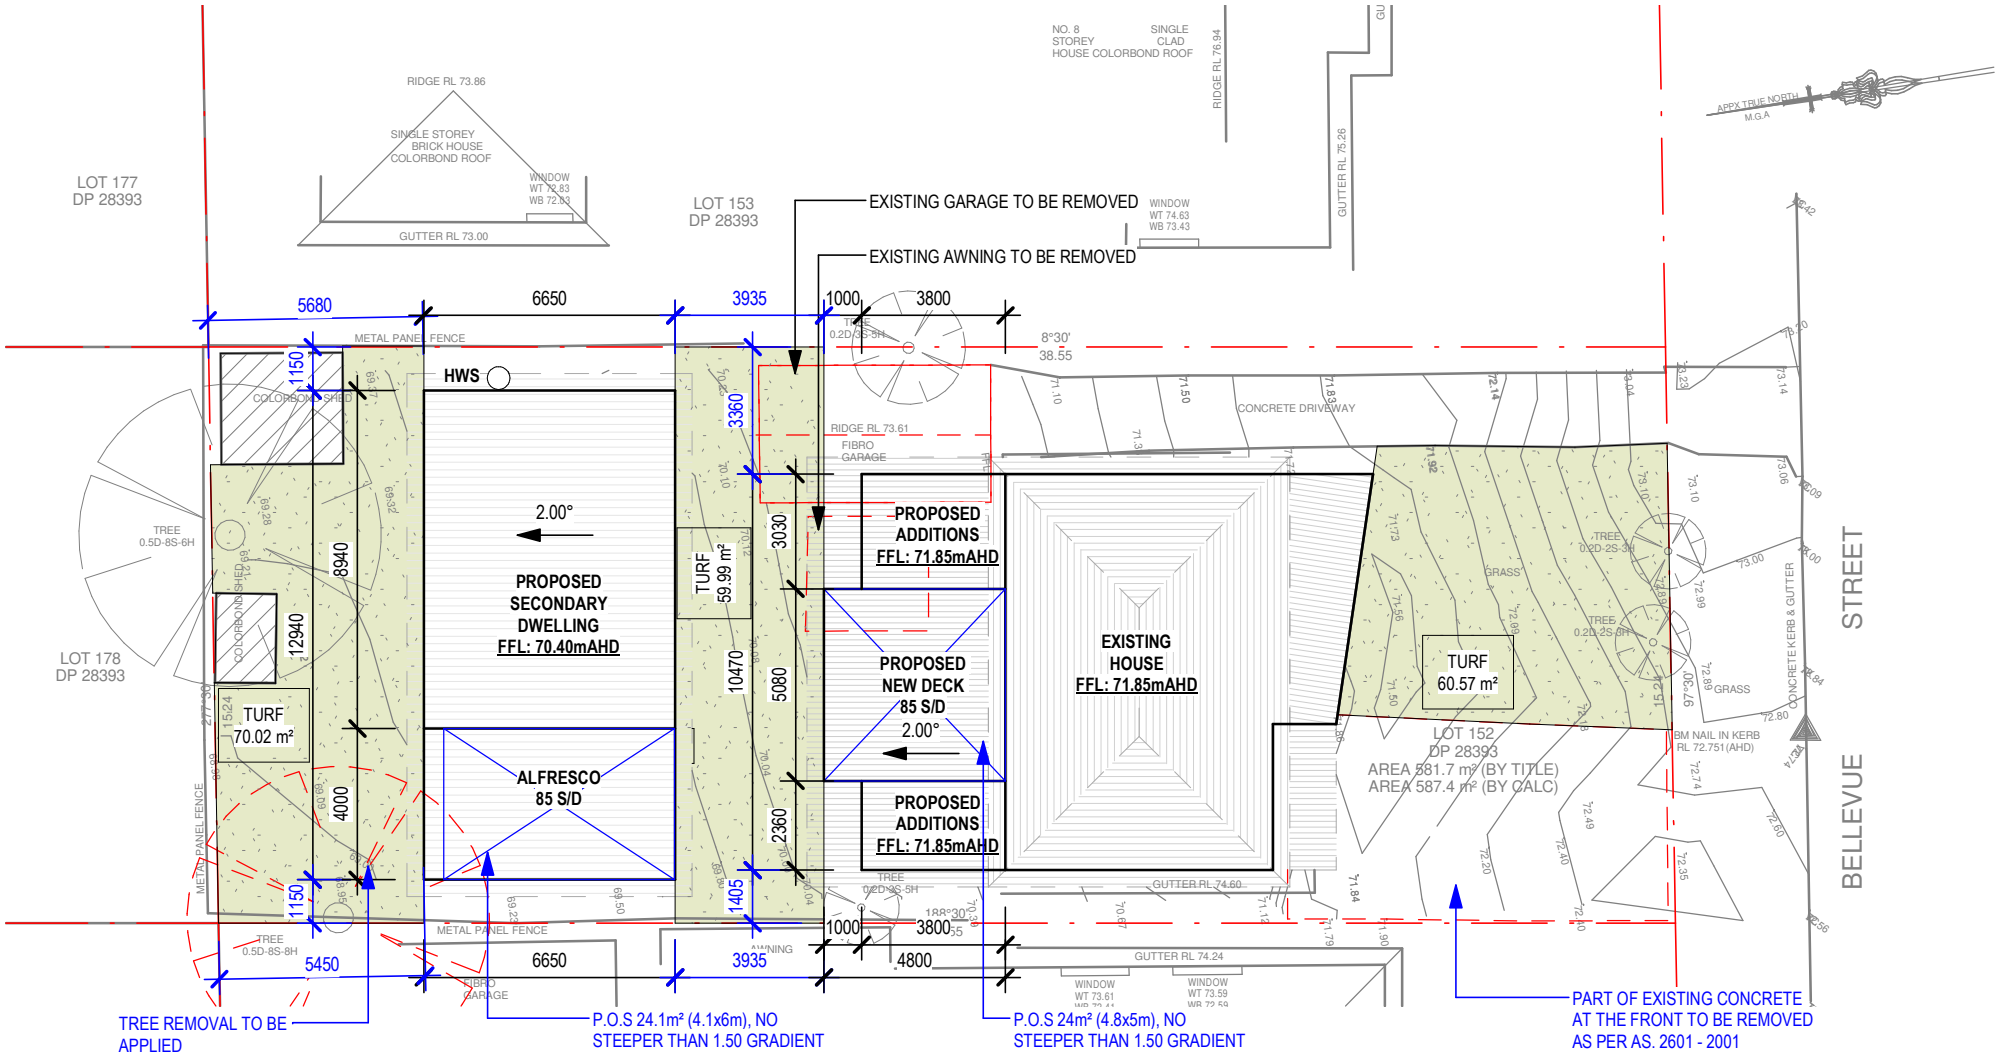

1 SITE & ROOF PLAN
1 : 200

© THIS DRAWING IS THE PROPERTY OF LT DESIGN & CONSULTING PTY LTD AND WE RESERVE THE COPYRIGHT TO ALL OUR DESIGNS WHICH CANNOT BE REPRODUCED (IN PART OR IN WHOLE) BEFORE FIRST OBTAINING WRITTEN CONSENT. CONTRAVENTION WILL BE PROSECUTED

• FIGURED DIMENSIONS TO BE TAKEN IN PREFERENCE TO SCALE.

• BUILDERS' WORK TO COMPLY WITH THE LATEST BCA AND ITS AMENDMENTS AND RELEVANT AUSTRALIAN STANDARDS REFERRED WITHIN.

No.	Description	Date



Building Design | 3D Modeling | Drafting | Detailing



BUILDING DESIGNERS AUSTRALIA

Accreditation No: 6302
Shop 6A/80 Thorney Rd, Fairfield West
0414 891 998 - Le@LTDesign.net.au

DRAWING:
SITE/ROOF PLAN

CLIENT & PROJECT: LOT 152 IN DP 28393
DEMOLITION OF EXISTING AWNING & GARAGE & PROPOSED SECONDARY DWELLING AND NEW ADDITIONS TO EXIST. HOUSE
AT: NO.6 BELLEVUE STREET, BLACKTOWN

COMPLYING DEVELOPMENT CERTIFICATE

DATE:
16/04/2026
DWG NO:
GF-0126-01



DRW BY:
LT

SCALE: As indicated (A3)

PROVIDE 1800mm HIGH SAFETY & SECURITY FENCE FOR THE DURATION OF THE DEMOLITION & CONSTRUCTION WORKS. SILT FENCE, GEOTEXTILE FABRIC OR THE EQUIVALENT TO ALL BOUNDARIES

ANY DAMAGE TO EXISTING &/OR ADJOINING
PROPERTY &/OR SERVICES IS TO BE MADE
GOOD WITH MINIMAL IF ANY
INCONVENIENCE TO ALL PROPRIETORS. IF
ANY DAMAGE IS DUE TO NEGLIGENCE, IT IS
TO BE RECTIFIED AT THE COST OF THE
NEGLIGENT PARTY WHICH CAUSED THAT
DAMAGE.

METHOD OF SUPPORT OF
EXCAVATION ADJACENT TO
ADJOINING PROPERTIES TO ENG'S
DETAILS AND IT IS TO BE CERTIFIED
BY A CERTIFIER ACCREDITED IN
CIVIL ENGINEERING


VEHICLES CARRYING LOOSE BUILDING MATERIALS TO BE COVERED IN COMPLIANCE WITH ROAD TRAFFIC REGULATIONS. SAFE ACCESS FOR HEAVY EQUIPMENT PLANT AND MATERIALS DELIVERY.

DEMOLISH & REMOVE FROM THE SITE. AS PER THE SPECIFICATION, THE COUNCIL REQUIREMENTS & AS. 2601 ALL THE EXISTING BUILDINGS, CARPORT, FENCES, DRIVEWAY, PATHS AND THE LIKE, AS SHOWN HATCHED AND/OR AS REQUIRED TO ACHIEVE THE PROPOSED WORK. DISCONNECT, CAP OFF & SEAL ALL REDUNDANT SERVICES PRIOR TO THE COMMENCEMENT OF DEMOLITION

LEGEND:



TO BE DEMOLISHED TO
COMPLY WITH AS 2601-2001

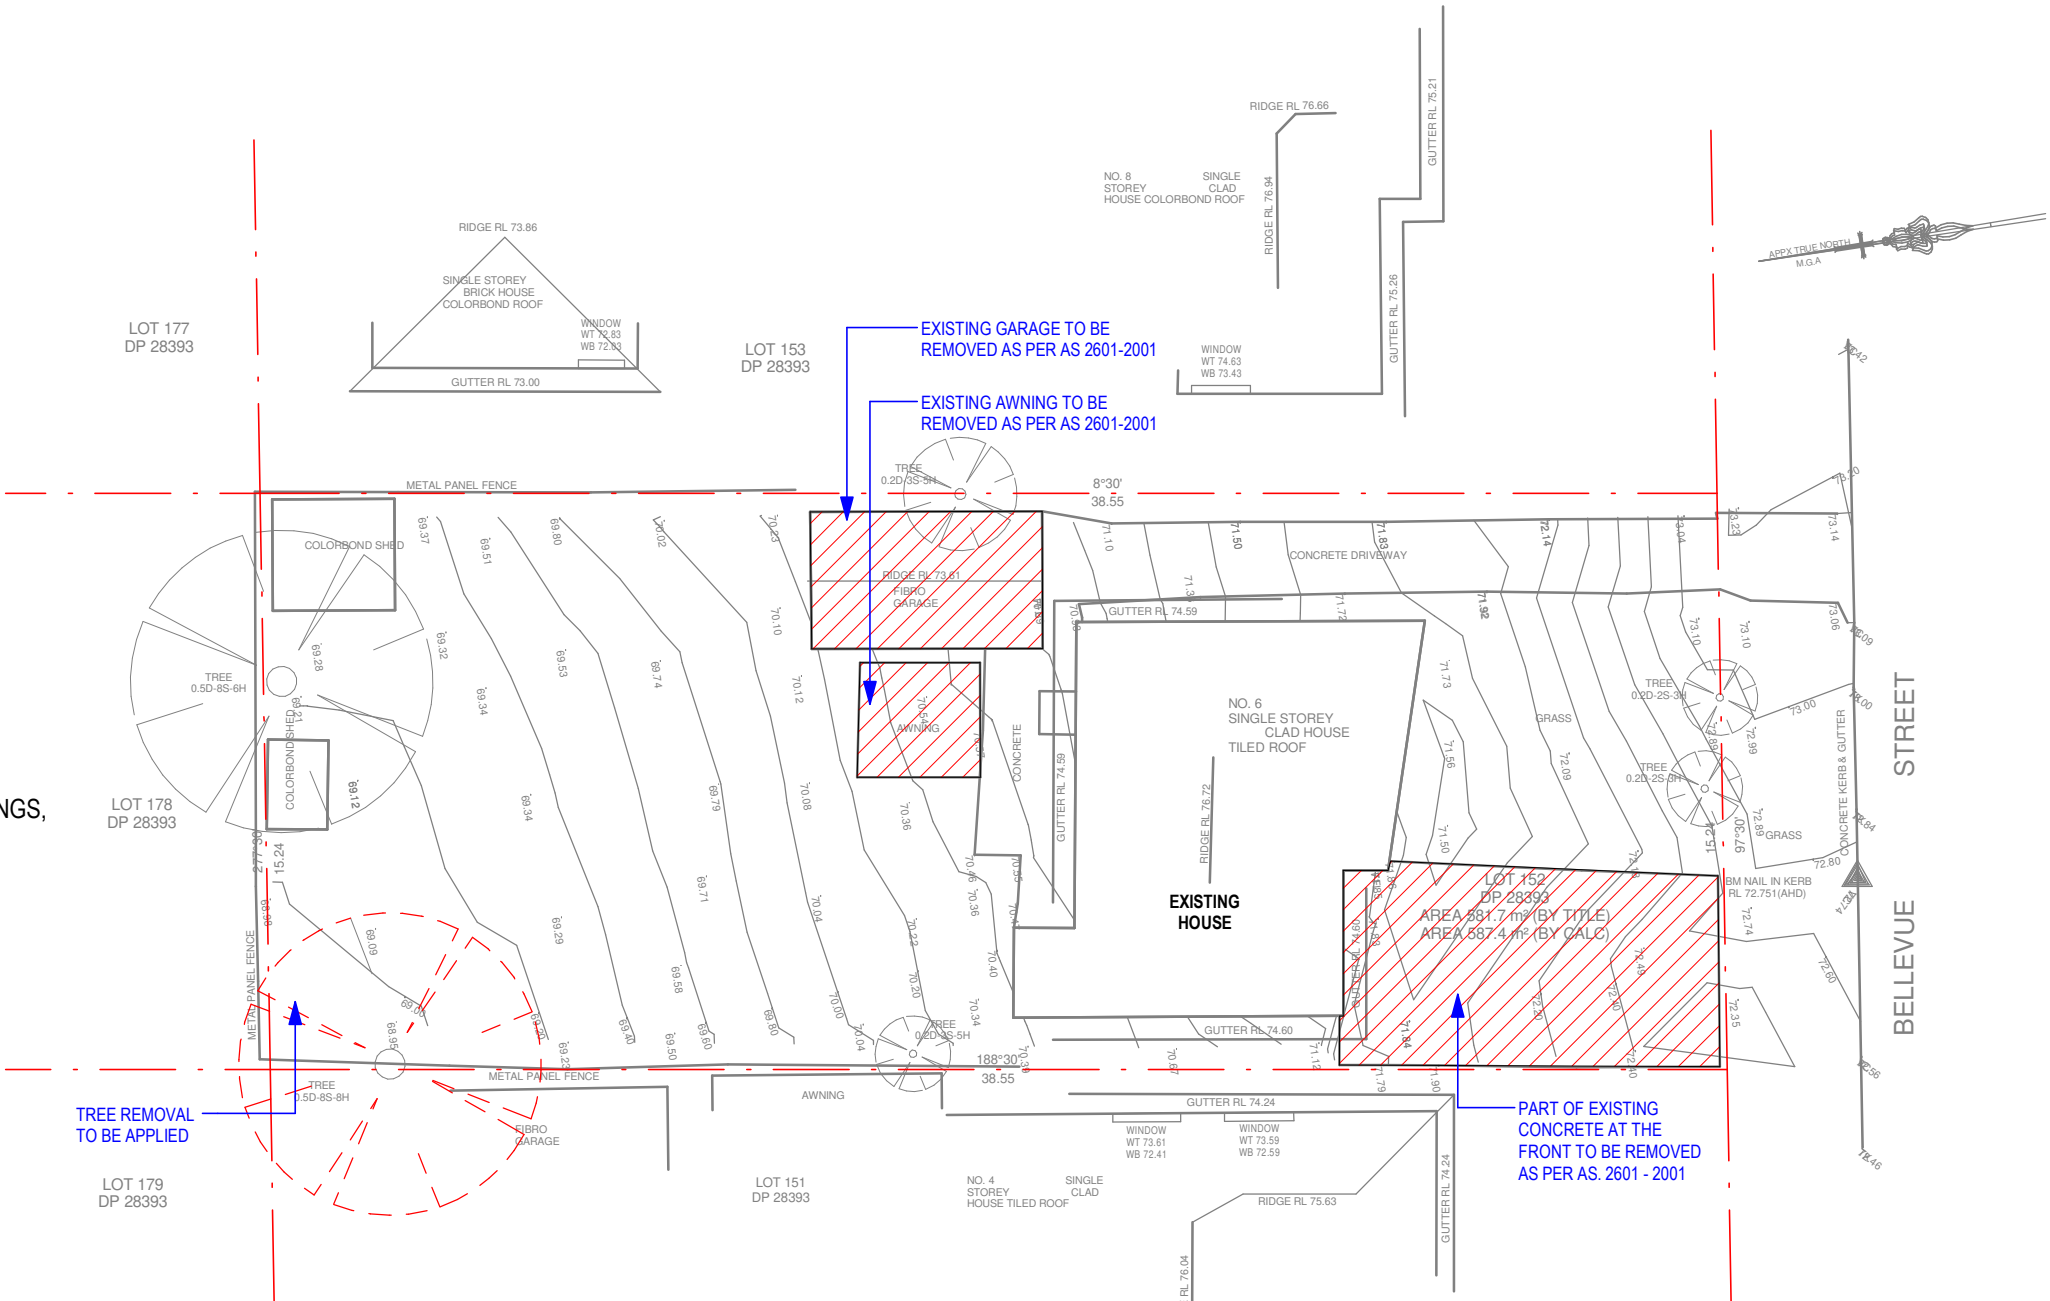

© THIS DRAWING IS THE PROPERTY OF LT DESIGN & CONSULTING PTY LTD AND WE RESERVE THE COPYRIGHT TO ALL OUR DESIGNS WHICH CANNOT BE REPRODUCED (IN PART OR IN WHOLE) BEFORE FIRST OBTAINING WRITTEN CONSENT. CONTRAVENTION WILL BE PROSECUTED

- FIGURED DIMENSIONS TO BE TAKEN IN PREFERENCE TO SCALE.
- BUILDERS' WORK TO COMPLY WITH THE LATEST BCA AND ITS AMENDMENTS AND RELEVANT AUSTRALIAN STANDARDS REFERRED WITHIN.

[illegible]

Building Design | 3D Modeling | Drafting | Detailing



**BUILDING
DESIGNERS
AUSTRALIA**

Accreditation No: 6302
Shop 6A/80 Thorney Rd, Fairfield West
0414 891 998 - Le@LTDesign.net.au

DRAWING: EXISTING AND DEMOLITION PLAN

CLIENT & PROJECT: LOT 152 IN DP 28393
DEMOLITION OF EXISTING AWNING & GARAGE & PROPOSED
SECONDARY DWELLING AND NEW ADDITIONS TO EXIST. HOUSE
AT: NO.6 BELLEVUE STREET, BLACKTOWN


COMPLYING DEVELOPMENT CERTIFICATE

DATE:
16/04/2026

DWG NO:
GF-0126-02

SCALE: 1 : 200 (A3)



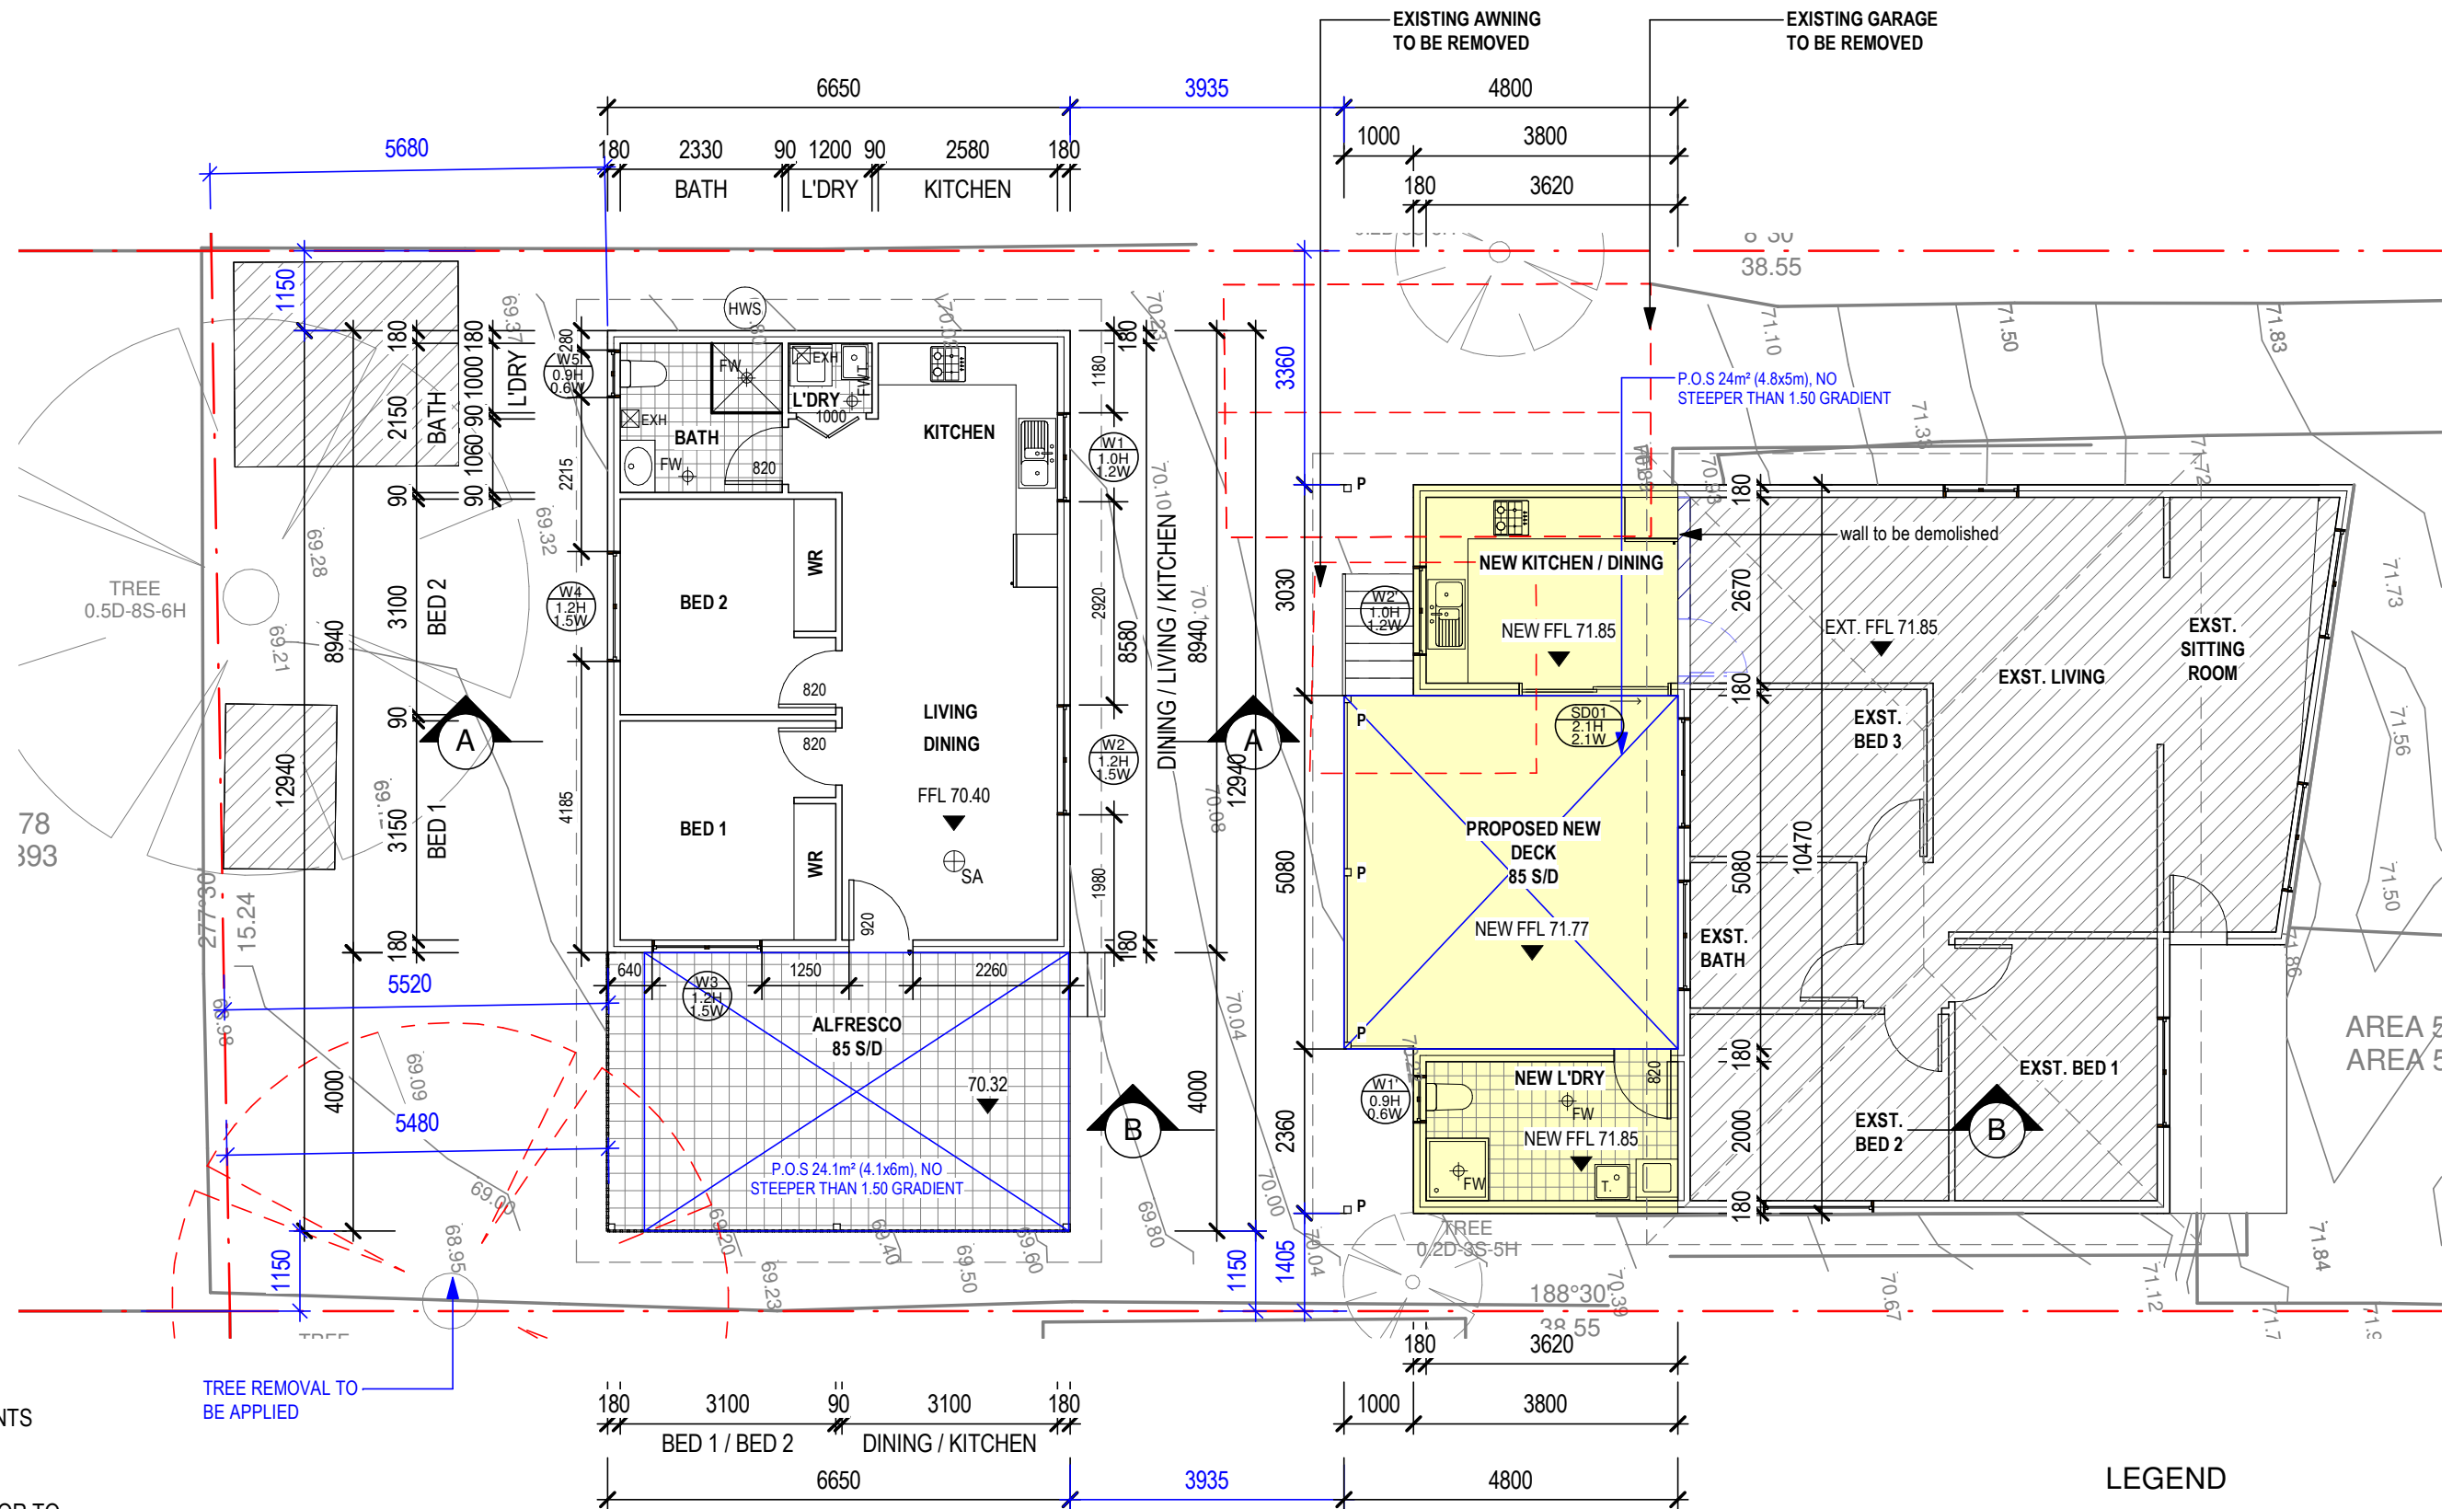

- VJ : VERTICAL BRICK JOINTS
WH : WEEPHOLES
LOH : LIFT OFF HINGES DOOR TO COMPLY WITH NCC 2022
SA : SMOKE ALARM TO COMPLY WITH AS.3786
FW : FLOOR WASTE
EXH : MECHANICAL VENTILATION SYSTEM

1 PROPOSED GROUND FLOOR PLAN
1 : 100

LEGEND

- EXISTING BUILDING
EXISTING WALL / STRUCTURES
EXISTING WALL TO BE DEMOLISHED
NEW WALL

© THIS DRAWING IS THE PROPERTY OF LT DESIGN & CONSULTING PTY LTD AND WE RESERVE THE COPYRIGHT TO ALL OUR DESIGNS WHICH CANNOT BE REPRODUCED (IN PART OR IN WHOLE) BEFORE FIRST OBTAINING WRITTEN CONSENT. CONTRAVENTION WILL BE PROSECUTED

• FIGURED DIMENSIONS TO BE TAKEN IN PREFERENCE TO SCALE.

• BUILDERS' WORK TO COMPLY WITH THE LATEST BCA AND ITS AMENDMENTS AND RELEVANT AUSTRALIAN STANDARDS REFERRED WITHIN.

No.	Description	Date



Building Design | 3D Modeling | Drafting | Detailing



BUILDING DESIGNERS AUSTRALIA
Accreditation No: 6302
Shop 6A/80 Thorne Rd, Fairfield West
0414 891 998 - Le@LTDesign.net.au

DRAWING:

PROPOSED GROUND FLOOR PLAN

CLIENT & PROJECT: LOT 152 IN DP 28393
DEMOLITION OF EXISTING AWNING & GARAGE & PROPOSED SECONDARY DWELLING AND NEW ADDITIONS TO EXIST. HOUSE
AT: NO.6 BELLEVUE STREET, BLACKTOWN

COMPLYING DEVELOPMENT CERTIFICATE


DATE: 16/04/2026
DWG NO: GF-0126-03
SCALE: 1 : 100 (A3)




DRW BY: LT

NOTE:
EAVES ENCROACHING WITHIN 900mm OF AN ALLOTMENT BOUNDARY AND 1800mm FROM ANOTHER BUILDING TO BE NON-COMBUSTILE


AC UNITS/HOT WATER UNITS/RWTS TO BE MINIMUM 450MM FROM BDY AND 900MM FROM ANOTHER BUILDING

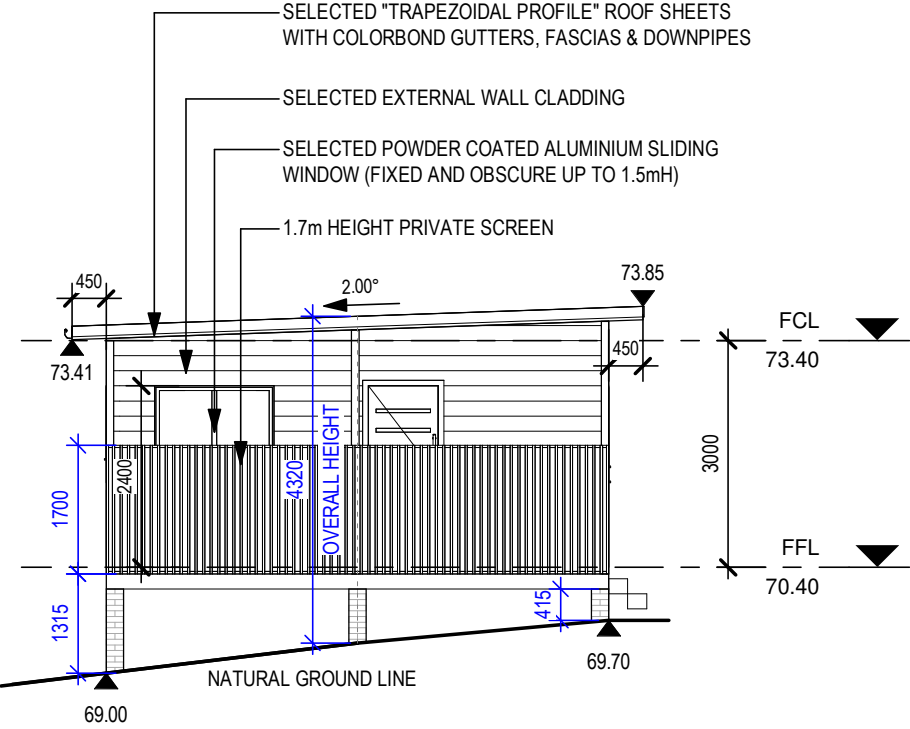


1 EAST ELEVATION
1 : 100

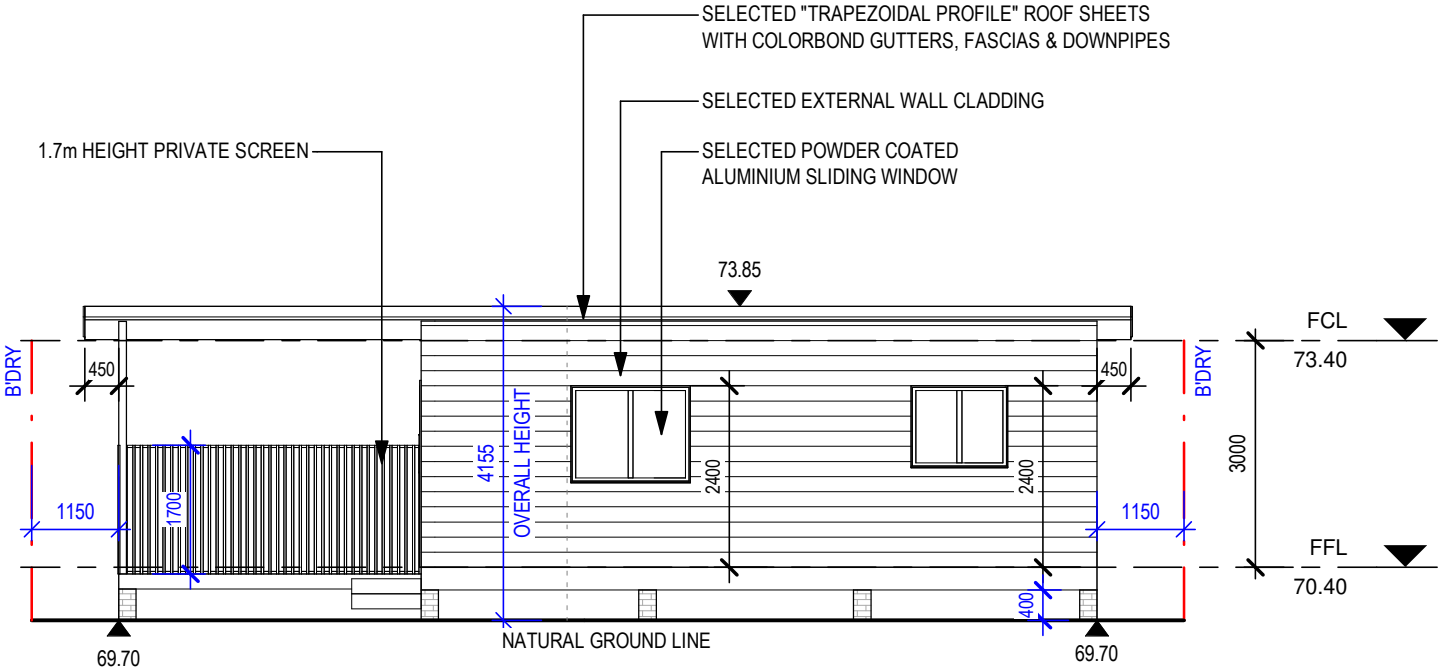

3 NORTH ELEVATION
1 : 100

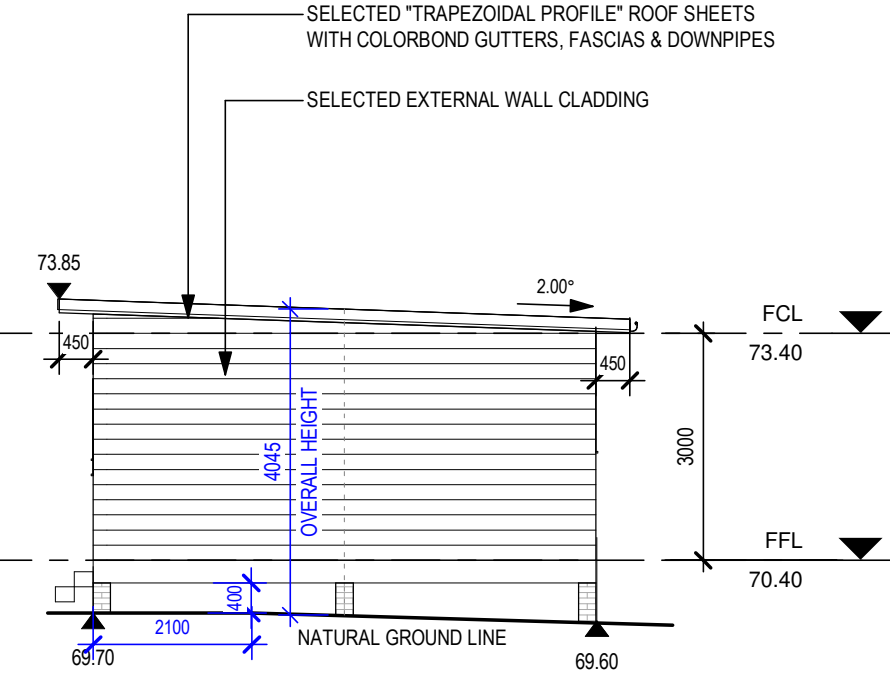

2 WEST ELEVATION
1 : 100

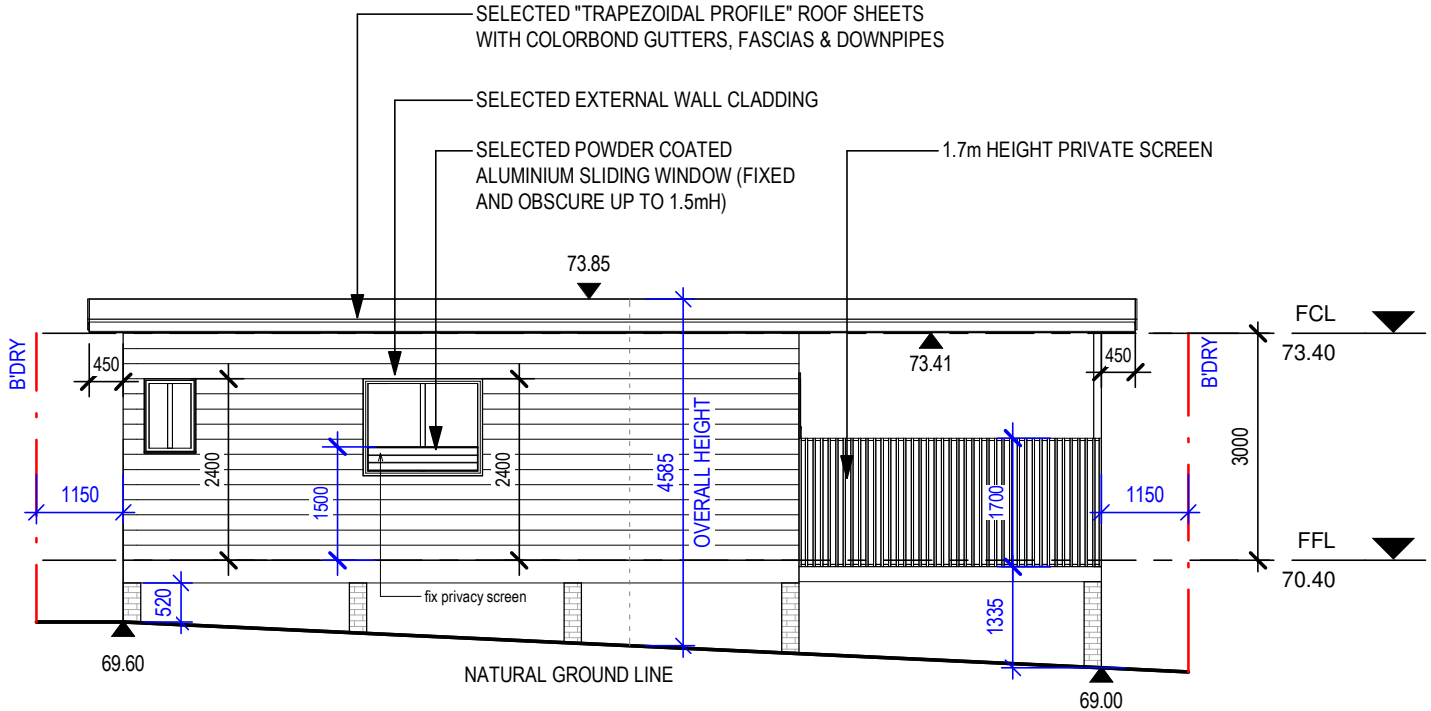

4 SOUTH ELEVATION
1 : 100

© THIS DRAWING IS THE PROPERTY OF LT DESIGN & CONSULTING PTY LTD AND WE RESERVE THE COPYRIGHT TO ALL OUR DESIGNS WHICH CANNOT BE REPRODUCED (IN PART OR IN WHOLE) BEFORE FIRST OBTAINING WRITTEN CONSENT. CONTRAVENTION WILL BE PROSECUTED

- FIGURED DIMENSIONS TO BE TAKEN IN PREFERENCE TO SCALE.
- BUILDERS' WORK TO COMPLY WITH THE LATEST BCA AND ITS AMENDMENTS AND RELEVANT AUSTRALIAN STANDARDS REFERRED WITHIN.

No.	Description	Date



Building Design | 3D Modeling | Drafting | Detailing



Accreditation No: 6302
Shop 6A/80 Thorney Rd, Fairfield West
0414 891 998 - Le@LTDesign.net.au

BUILDING
DESIGNERS
AUSTRALIA

DRAWING:
ELEVATIONS

CLIENT & PROJECT: LOT 152 IN DP 28393
DEMOLITION OF EXISTING AWNING & GARAGE & PROPOSED
SECONDARY DWELLING AND NEW ADDITIONS TO EXIST. HOUSE
AT: NO.6 BELLEVUE STREET, BLACKTOWN

COMPLYING DEVELOPMENT CERTIFICATE


DATE:
16/04/2026
DWG NO:
GF-0126-04

SCALE:




DRW BY:
LT


1 : 100 (A3)

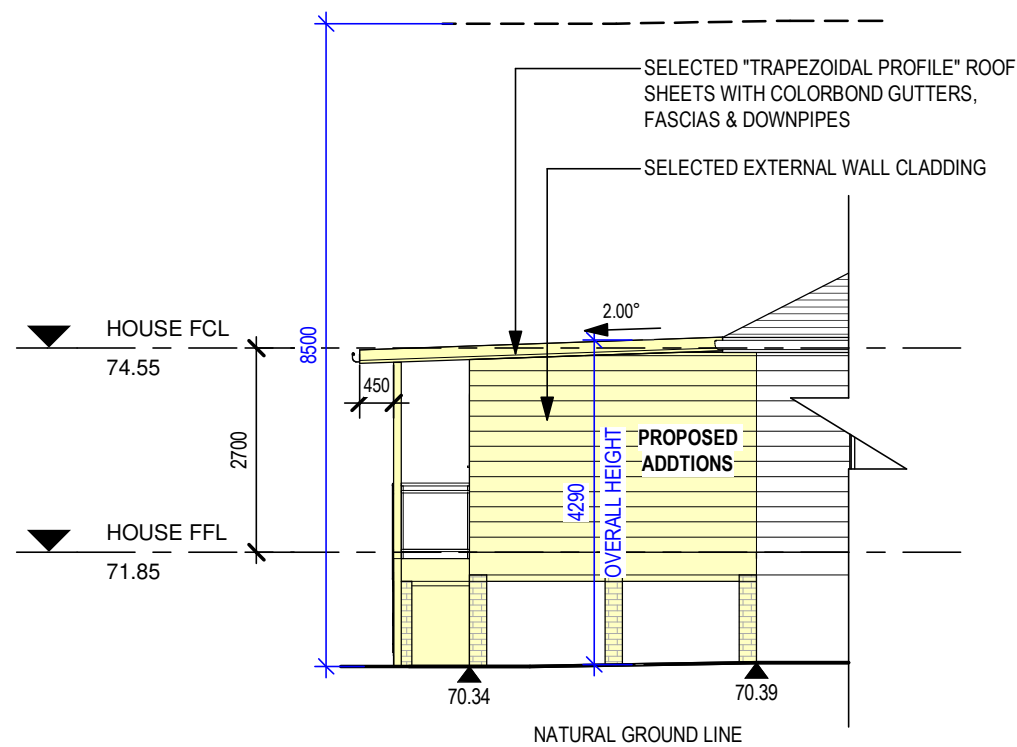

1 EAST ELEVATION
1 : 100

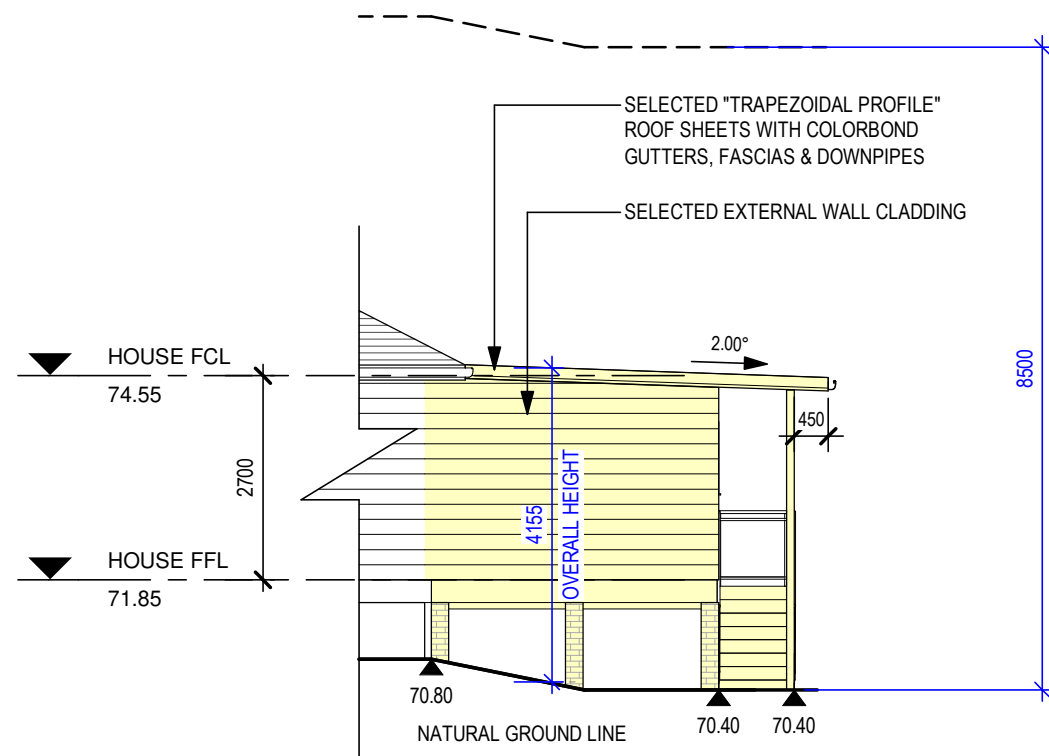

2 WEST ELEVATION
1 : 100

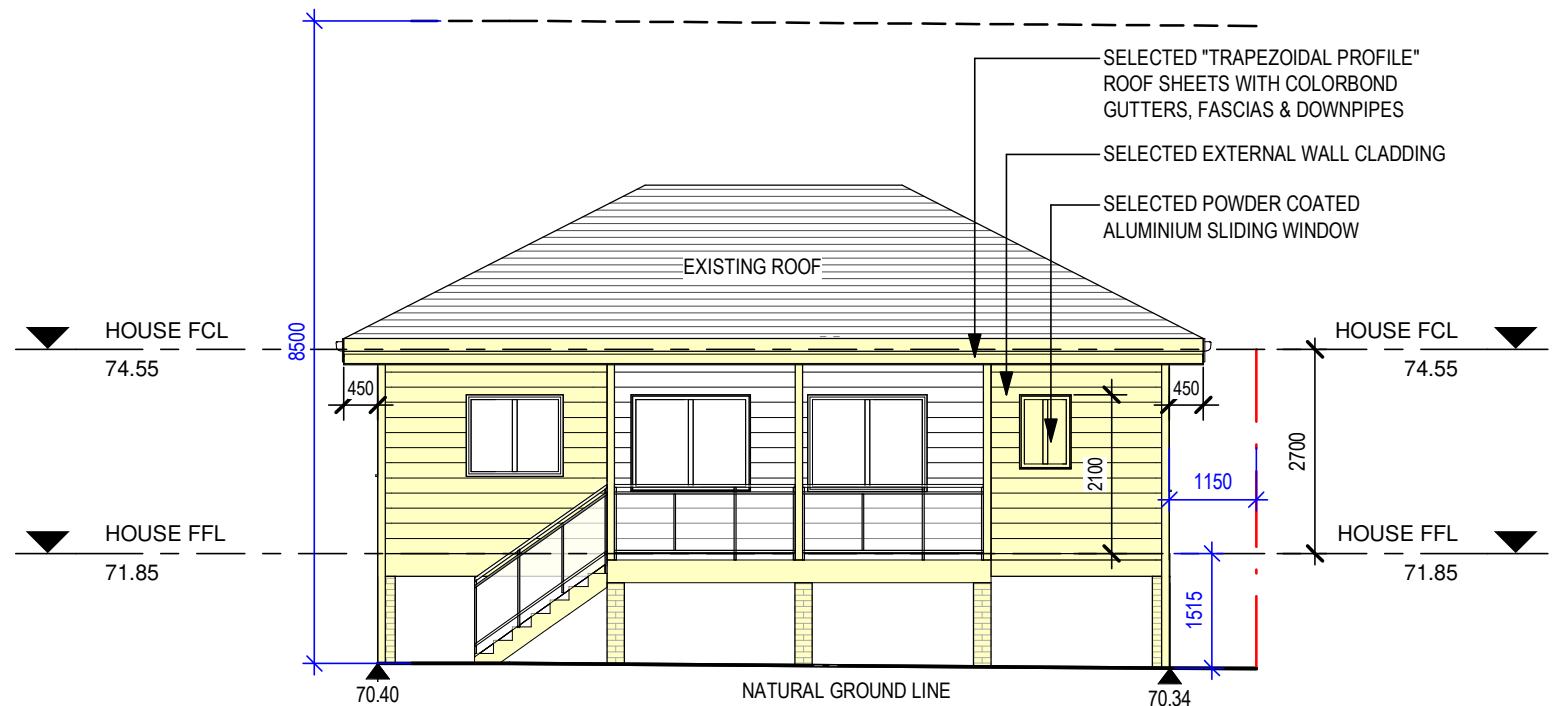

3 SOUTH ELEVATION
1 : 100

NOTE:
EAVES ENCROACHING WITHIN 900mm
OF AN ALLOTMENT BOUNDARY AND
1800mm FROM ANOTHER BUILDING TO
BE NON-COMBUSTILE

AC UNITS/HOT WATER UNITS/RWTS TO
BE MINIMUM 450MM FROM BDY AND
900MM FROM ANOTHER BUILDING

LEGEND

EXISTING BUILDING	
EXISTING WALL / STRUCTURES	
EXISTING WALL TO BE DEMOLISHED	
NEW WALL	

© THIS DRAWING IS THE PROPERTY OF LT DESIGN & CONSULTING PTY LTD AND WE RESERVE THE COPYRIGHT TO ALL OUR DESIGNS WHICH CANNOT BE REPRODUCED (IN PART OR IN WHOLE) BEFORE FIRST OBTAINING WRITTEN CONSENT. CONTRAVENTION WILL BE PROSECUTED

- FIGURED DIMENSIONS TO BE TAKEN IN PREFERENCE TO SCALE.
- BUILDERS' WORK TO COMPLY WITH THE LATEST BCA AND ITS AMENDMENTS AND RELEVANT AUSTRALIAN STANDARDS REFERRED WITHIN.

No.	Description	Date



Building Design | 3D Modeling | Drafting | Detailing



BUILDING DESIGNERS AUSTRALIA
Accreditation No: 6302
Shop 6A/80 Thorney Rd, Fairfield West
0414 891 998 - Le@LTDesign.net.au

DRAWING: ELEVATIONS (ADDITONS)

CLIENT & PROJECT: LOT 152 IN DP 28393
DEMOLITION OF EXISTING AWNING & GARAGE & PROPOSED SECONDARY DWELLING AND NEW ADDITIONS TO EXIST. HOUSE AT: NO.6 BELLEVUE STREET, BLACKTOWN

COMPLYING DEVELOPMENT CERTIFICATE

DATE:
16/04/2026
DWG NO:
GF-0126-05

SCALE:



DRW BY:
LT


1 : 100 (A3)

LEGEND


EXISTING BUILDING	
EXISTING WALL / STRUCTURES	
EXISTING WALL TO BE DEMOLISHED	
NEW WALL	

NOTE:
EAVES ENCROACHING WITHIN 900mm OF AN ALLOTMENT BOUNDARY AND 1800mm FROM ANOTHER BUILDING TO BE NON-COMBUSTILE


AC UNITS/HOT WATER UNITS/RWTS TO BE MINIMUM 450MM FROM BDY AND 900MM FROM ANOTHER BUILDING

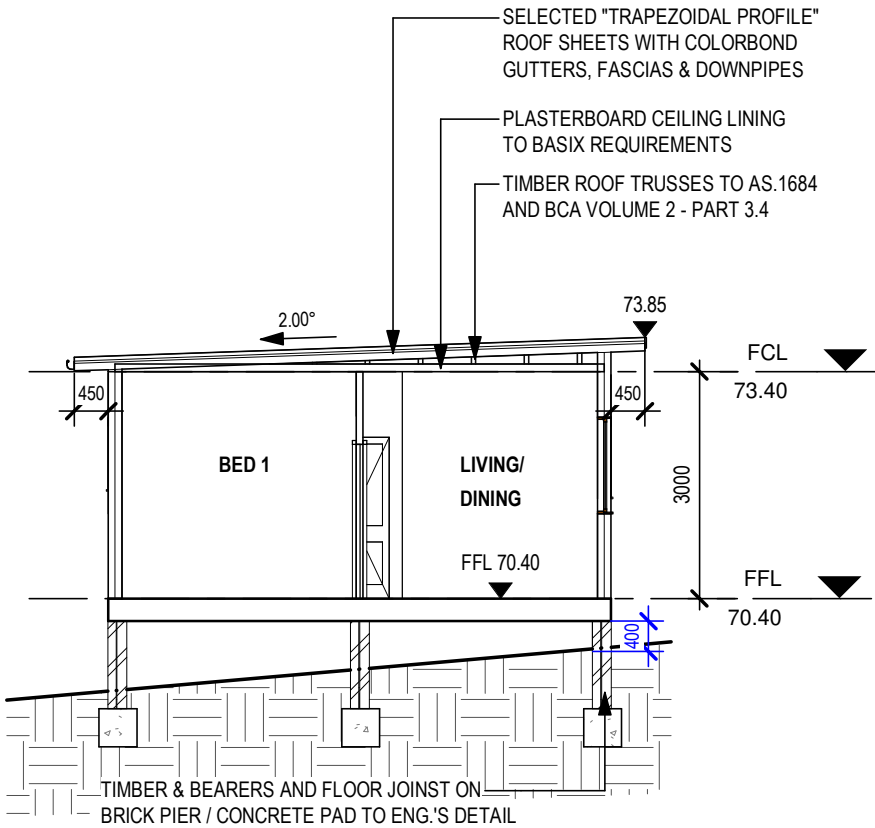

1 SECTION A-A
1 : 100

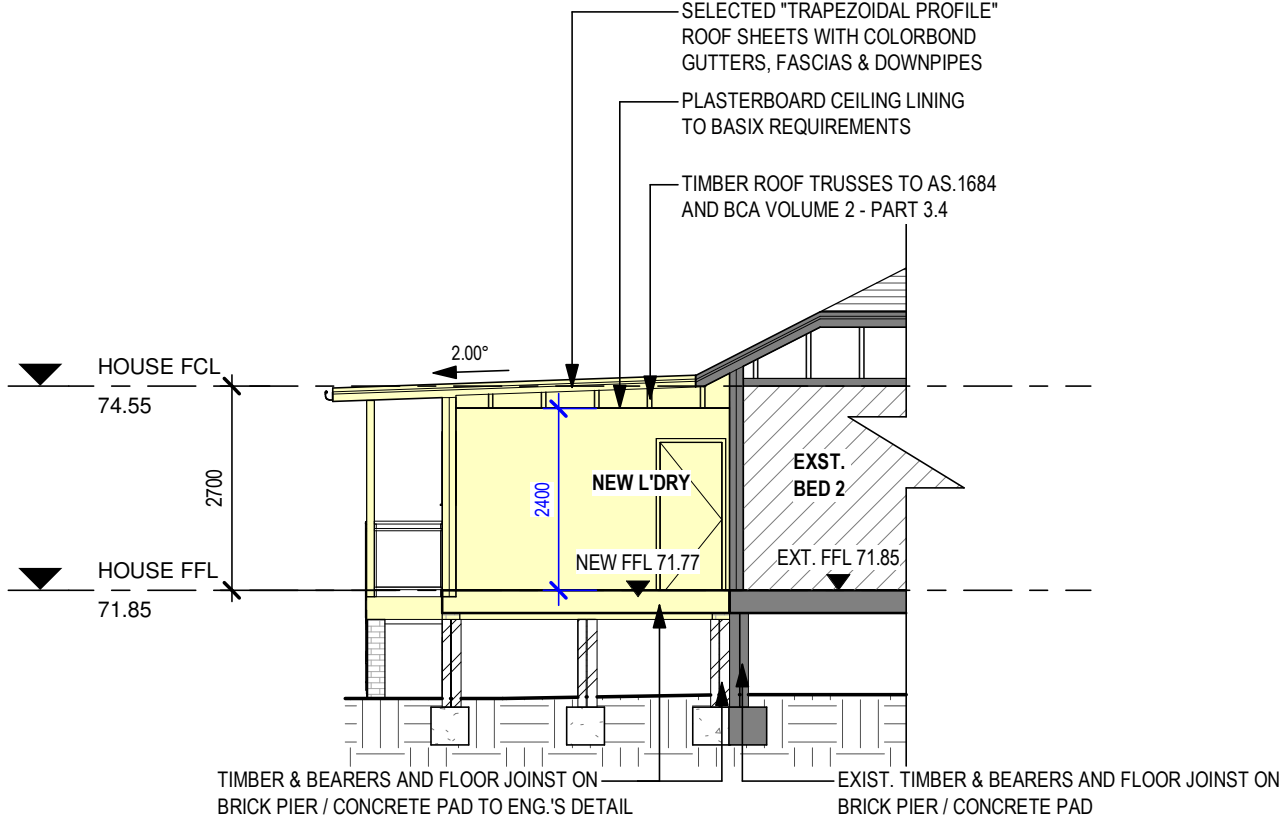

2 SECTION B-B
1 : 100

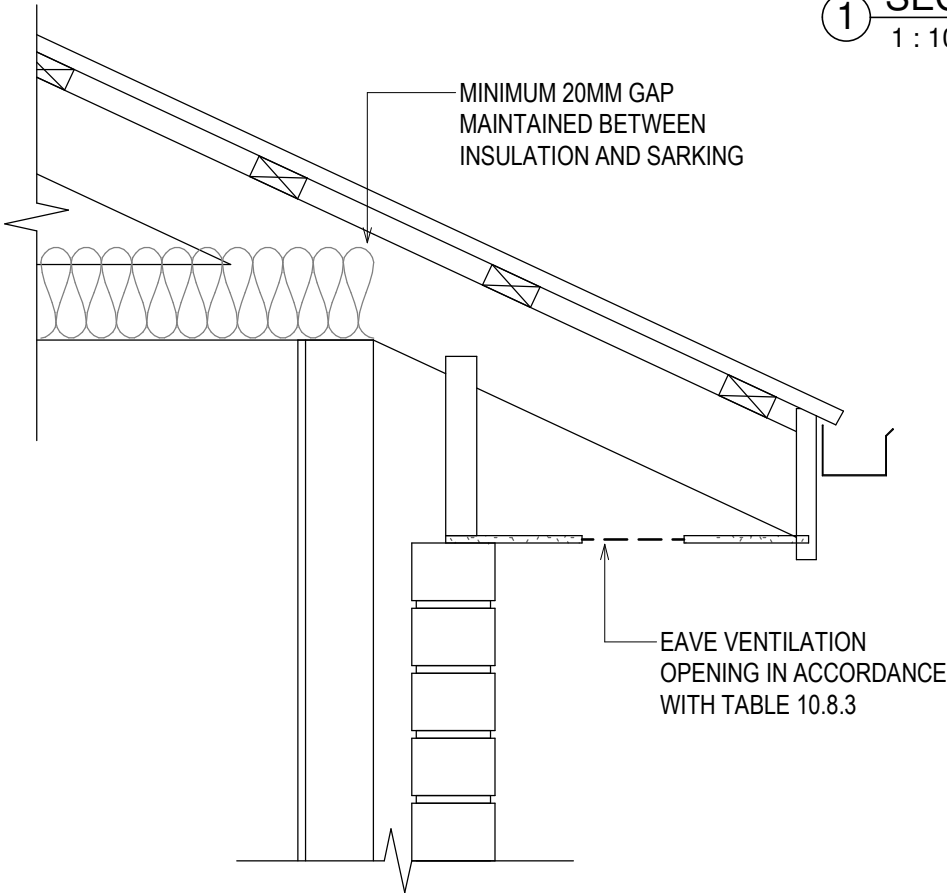

CONDENSATION MANAGEMENT DETAILS

7.2.3


Minimum pitches for metal sheet roofing profiles

[2019: 3.5.1.3]

Metal sheet roofing must comply with the minimum pitch requirements for the associated roof profile in accordance with Figure 7.2.3.

Figure 7.2.3:

Minimum pitch requirements for metal roofing profiles

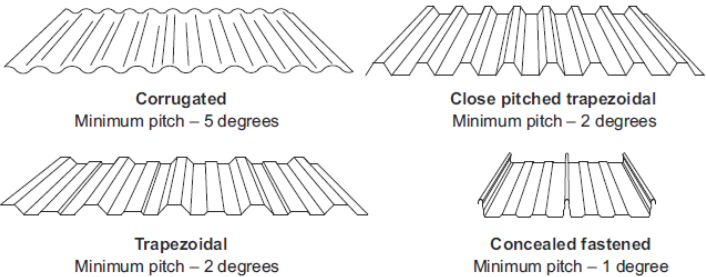

CONDENSATION MANAGEMENT

- (1)AN EXHAUST SYSTEM INSTALLED IN A KITCHEN, BATHROOM, SANITARY COMPARTMENT OR LAUNDRY MUST HAVE A MINIMUM FLOW RATE OF—
(A)25 L/S FOR A BATHROOM OR SANITARY COMPARTMENT; AND
(B)40 L/S FOR A KITCHEN OR LAUNDRY.
- (2)EXHAUST FROM A KITCHEN, KITCHEN RANGE HOOD, BATHROOM, SANITARY COMPARTMENT OR LAUNDRY MUST DISCHARGE DIRECTLY OR VIA A SHAFT OR DUCT TO OUTDOOR AIR.
- (3)WHERE A VENTING CLOTHES DRYER IS INSTALLED, IT MUST DISCHARGE DIRECTLY OR VIA A SHAFT OR DUCT TO OUTDOOR AIR.
- (4)AN EXHAUST SYSTEM THAT IS NOT RUN CONTINUOUSLY AND IS SERVING A BATHROOM OR SANITARY COMPARTMENT THAT IS NOT VENTILATED IN ACCORDANCE WITH 10.6.2(A) MUST—
(A)BE INTERLOCKED WITH THE ROOM'S LIGHT SWITCH; AND
(B)INCLUDE A RUN-ON TIMER SO THAT THE EXHAUST SYSTEM CONTINUES TO OPERATE FOR 10 MINUTES AFTER THE LIGHT SWITCH IS TURNED OFF.
- (5)EXCEPT FOR ROOMS THAT ARE VENTILATED IN ACCORDANCE WITH 10.6.2(A), A ROOM WITH AN EXHAUST SYSTEM IN ACCORDANCE WITH (1) MUST BE PROVIDED WITH MAKE-UP AIR—
(A)VIA OPENINGS TO AN ADJACENT ROOM WITH A FREE AREA OF 14,000 MM2; OR IN ACCORDANCE WITH AS 1668.2.

© THIS DRAWING IS THE PROPERTY OF LT DESIGN & CONSULTING PTY LTD AND WE RESERVE THE COPYRIGHT TO ALL OUR DESIGNS WHICH CANNOT BE REPRODUCED (IN PART OR IN WHOLE) BEFORE FIRST OBTAINING WRITTEN CONSENT. CONTRAVENTION WILL BE PROSECUTED

• FIGURED DIMENSIONS TO BE TAKEN IN PREFERENCE TO SCALE.

• BUILDERS' WORK TO COMPLY WITH THE LATEST BCA AND ITS AMENDMENTS AND RELEVANT AUSTRALIAN STANDARDS REFERRED WITHIN.

No.	Description	Date



Building Design | 3D Modeling | Drafting | Detailing



BUILDING DESIGNERS AUSTRALIA
Accreditation No: 6302
Shop 6A/80 Thorney Rd, Fairfield West
0414 891 998 - Le@LTDesign.net.au

DRAWING:
SECTIONS

CLIENT & PROJECT: LOT 152 IN DP 28393
DEMOLITION OF EXISTING AWNING & GARAGE & PROPOSED SECONDARY DWELLING AND NEW ADDITIONS TO EXIST. HOUSE
AT: NO.6 BELLEVUE STREET, BLACKTOWN

COMPLYING DEVELOPMENT CERTIFICATE

DATE:
16/04/2026
DWG NO:
GF-0126-06



DRW BY:
LT





SCALE: As indicated (A3)

NOTES

- 1. NO VEHICLE CROSSING OR STOCKPILING OF MATERIAL SHOULD OCCUR ON THE VEGETATED BUFFER.
- 2. ALL SEDIMENT CONTROL STRUCTURES SHOULD BE INSPECTED & MAINTAINED BY THE SITE MANAGE DAILY
- 3. ALL SEDIMENT RETAINING STRUCTURES SHOULD BE CLEANED ON REACHING 50% STORAGE CAPACITY. SEDIMENT REMOVED SHOULD BE SPREAD WITHIN THE DISTURBED AREA.
- 4. ALL EXISTING VEGETATION ON THE SITE PERIMETER MUST BE RETAINED.
- 5. ROOF GUTTERS AND DOWNPIPES MUST BE CONNECT TO THE SITE DRAINAGE IMMEDIATELY AFTER ROOF CONSTRUCTION.
- 6. ALL DISTURBED AREA ARE TO BE RE-VEGETATED OR STABILISEED TO PREVENT EROSION. I.E. LANDSCAPING/ MULCHING/ TURFING.
- 7. MATERIALS AREA NOT TO BE STORED ON THE FOOTPATH.

GENERAL LEGEND

- SILT FENCE
- STOCKPILE
- MATERIAL STORAGE
- WASTE STORAGE & RECYCLING AREA
- GARBAGE BIN
- ONSITE TOILET
- ACCESS FOR VEHICLES

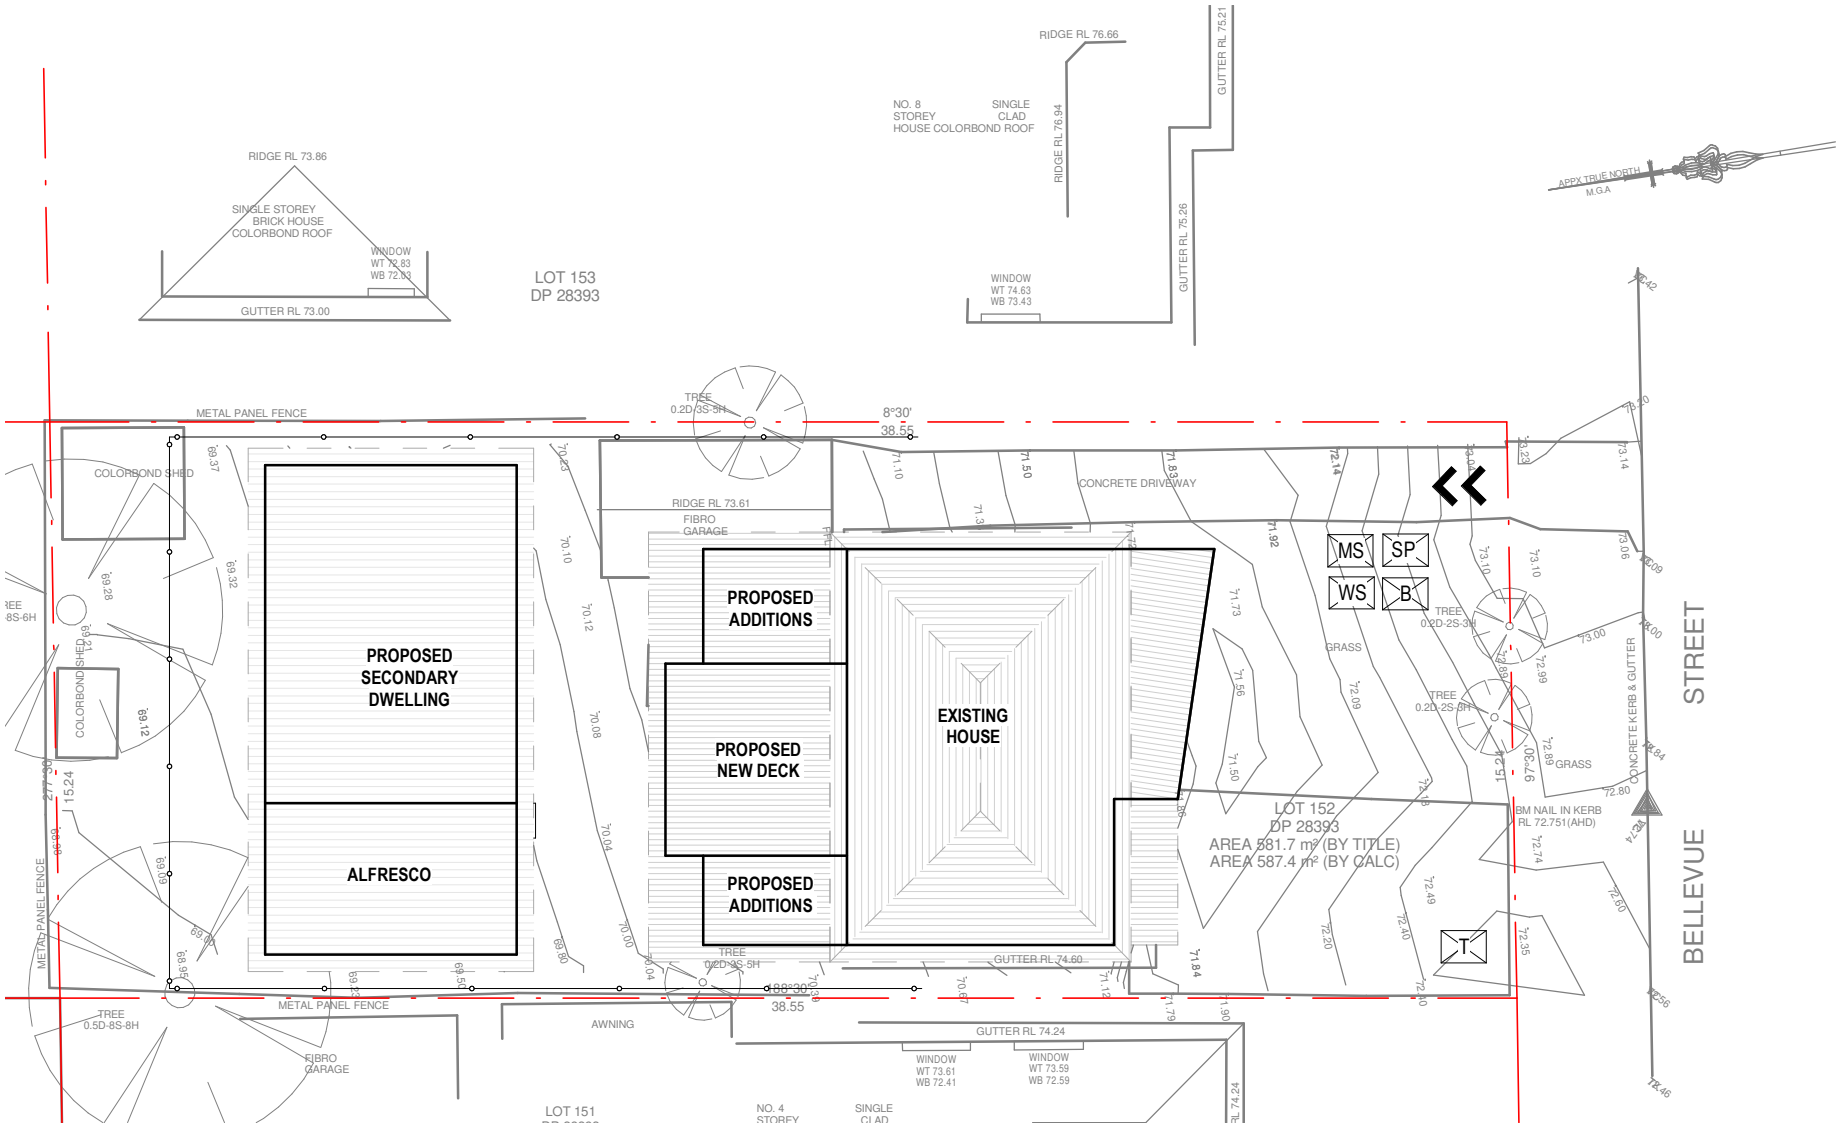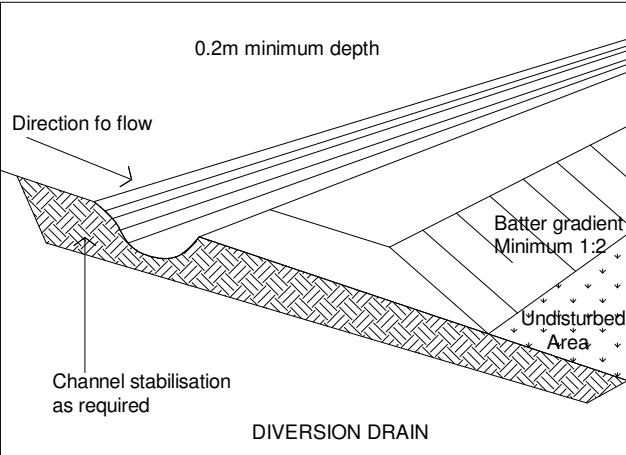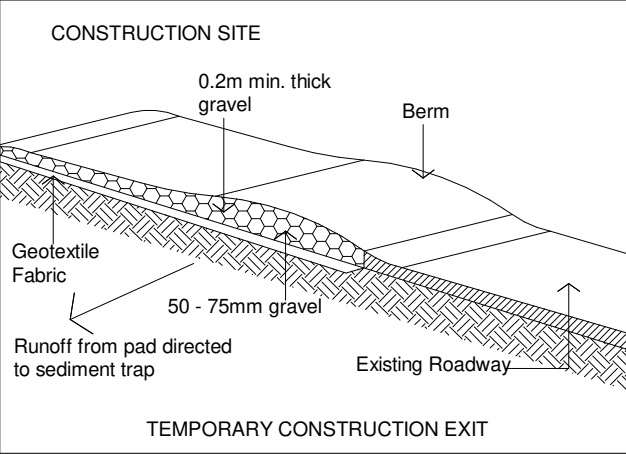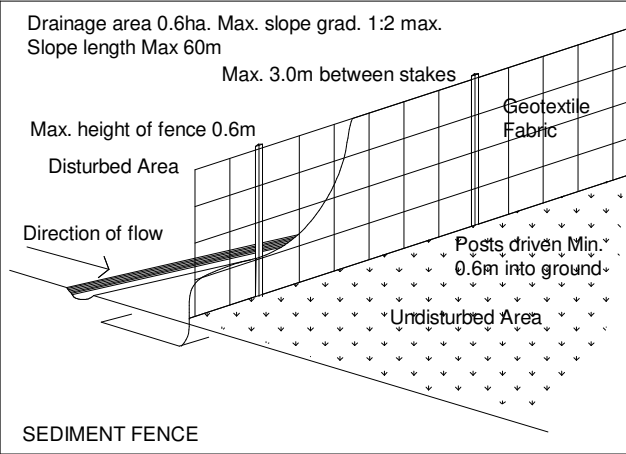

1 EROSION AND SEDIMENT CONTROL PLAN
1 : 200

© THIS DRAWING IS THE PROPERTY OF LT DESIGN & CONSULTING PTY LTD AND WE RESERVE THE COPYRIGHT TO ALL OUR DESIGNS WHICH CANNOT BE REPRODUCED (IN PART OR IN WHOLE) BEFORE FIRST OBTAINING WRITTEN CONSENT. CONTRAVENTION WILL BE PROSECUTED

- FIGURED DIMENSIONS TO BE TAKEN IN PREFERENCE TO SCALE.
- BUILDERS' WORK TO COMPLY WITH THE LATEST BCA AND ITS AMENDMENTS AND RELEVANT AUSTRALIAN STANDARDS REFERRED WITHIN.

No.	Description	Date



Building Design | 3D Modeling | Drafting | Detailing



BUILDING DESIGNERS AUSTRALIA

Accreditation No: 6302
Shop 6A/80 Thorney Rd, Fairfield West
0414 891 998 - Le@LTDesign.net.au

DRAWING:
EROSION & SEDIMENT CONTROL PLAN

CLIENT & PROJECT: LOT 152 IN DP 28393
DEMOLITION OF EXISTING AWNING & GARAGE & PROPOSED SECONDARY DWELLING AND NEW ADDITIONS TO EXIST. HOUSE
AT: NO.6 BELLEVUE STREET, BLACKTOWN

COMPLYING DEVELOPMENT CERTIFICATE

DATE:
16/04/2026
DWG NO:
GF-0126-07

SCALE: As indicated (A3)



DRW BY:
LT

Building Sustainability Index www.basix.nsw.gov.au

"The specifications provided below outline water, thermal performance, material, and energy commitments as per the BASIX certificate. Any discrepancies between the drawings, this summary table, and the original BASIX certificate must be reported immediately to the designer. Always refer to the original BASIX certificate for building construction, materials, insulation requirements, and other details. Please do not solely rely on this summary table, as it only highlights the essential criteria for the purpose of approval."

Showerheads Sytem: Min. 4 star Kitchen Taps: Min. 3 star
Toilet Flushing Sysmtem: Min. 3 star Basin Taps: Min. 3 star
Rainwater Tank: --

Material: Framed (fibre cement sheet or boards) Insulation: R3.0 (or 3.5 incl. const.)
Wall Colour: Light

Glazing: Clear Glazing	Frame : Standard Aluminium	Internal cover: Blinds
Eaves: 450mm	Window Frame / Glass Specs: Ref. to Basix for details	

Material: Colorbond Roof Type: Flat Roof
Roof Colour: Medium (solar absorptance 0.48- 0.59) Insulation: foil/sarking

Covering: not specified
Materials: suspended floor above enclosed subfloor, treated softwood;
frame: timber - H2 treated softwood.
Insulation: 2 (or 2.7 including construction) (down)

Hotwater unit : Gas instantaneous with a performance of 5 stars
Cooling / Heating System: A/C System 3 star
Ventilation System: Mechanical Vent. System to Kitchen, Bathroom and Laundry
Outdoor Clothes Drying

Building Sustainability Index www.basix.nsw.gov.au

"The specifications provided below outline water, thermal performance, material, and energy commitments as per the BASIX certificate. Any discrepancies between the drawings, this summary table, and the original BASIX certificate must be reported immediately to the designer. Always refer to the original BASIX certificate for building construction, materials, insulation requirements, and other details. Please do not solely rely on this summary table, as it only highlights the essential criteria for the purpose of approval."

Showerheads Sytem: Min. 3 star Kitchen Taps: Min. 3 star
Toilet Flushing Sysmtem: Min. 3 star Basin Taps: Min. 3 star
Rainwater Tank: --

Material: Framed ((weatherboard, fibro, metal clad) Insulation: R1.30 (or R1.70 including construction)
Wall Colour: Light

Glazing: Clear Glazing	Frame : Standard Aluminium	Internal cover: Blinds
Eaves: 450mm	Window Frame / Glass Specs: Ref. to Basix for details	

Material: Colorbond Roof Type: Flat Roof
Roof Colour: Medium (solar absorptance 0.48- 0.59) Insulation: foil/sarking

Material: Plasterboard Insulation: R3.5 (up)
Ceiling Fan: in living room

Covering: not specified
Materials: suspended floor with open subfloor: framed (R0.7).
Insulation: R1.3 (down) (or R2.00 including construction)





Hotwater unit : Gas instantaneous with a performance of 5 stars
Cooling / Heating System: A/C System 3 star
Ventilation System: Mechanical Vent. System to Kitchen, Bathroom and Laundry
Outdoor Clothes Drying

- BUILDERS' WORK TO COMPLY WITH THE LATEST BCA AND ITS AMENDMENTS AND RELEVANT AUSTRALIAN STANDARDS REFERRED WITHIN.

DESIGN


Accreditation No: 6302
Shop 6A/80 Thorney Rd, Fairfield West
0414 891 998 - Le@LTDesign.net.au

: 200 (A3)

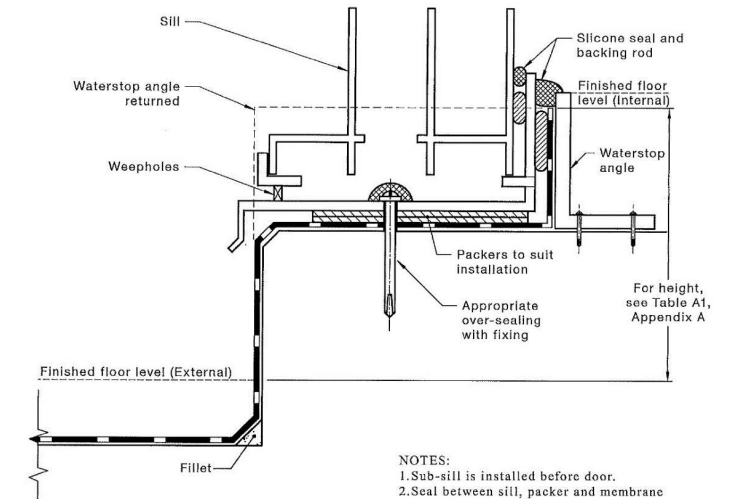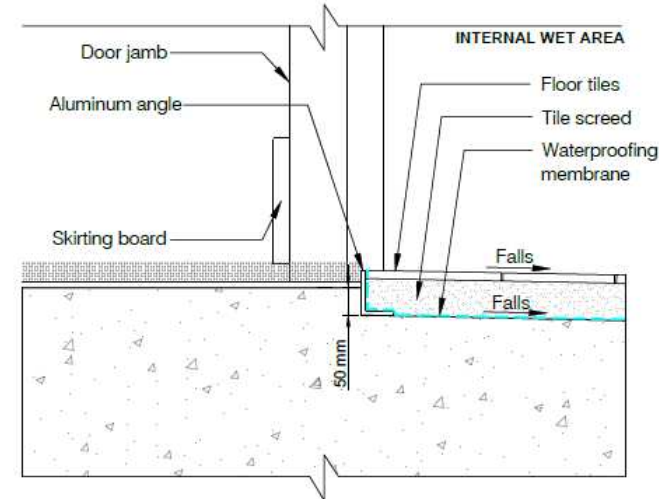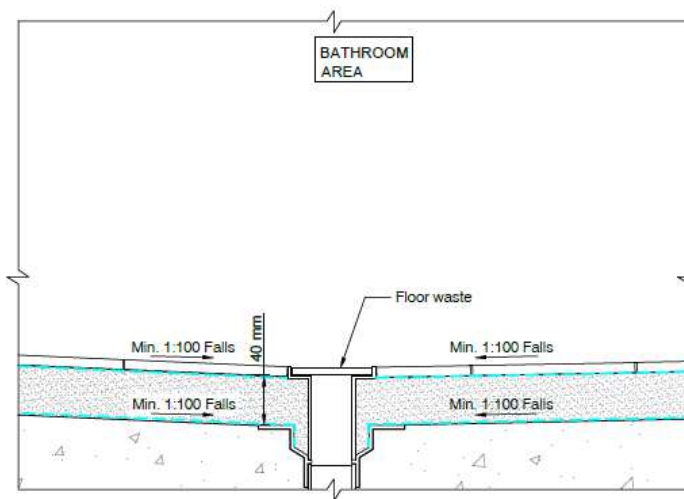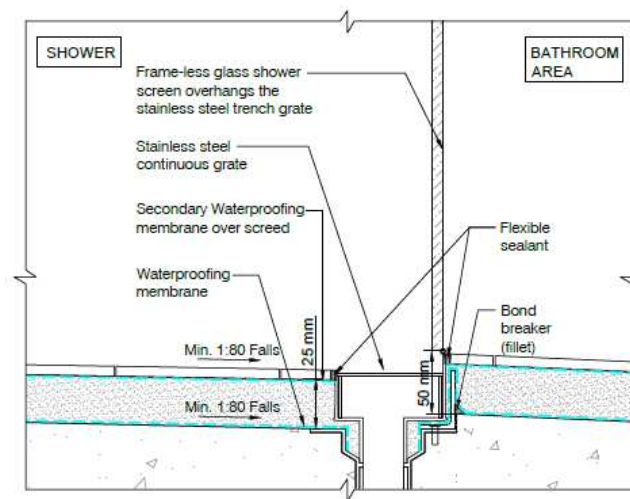


NOTES:
1. Sub-sill is installed before door.
2. Seal between sill, packer and membrane before drilling fixing holes.

MV DISCHARGE TO EXTERNAL WALL
(MUST REMAIN RUNNING FOR 10
MINUTES AFTER SWITCH IS ON-OFF)

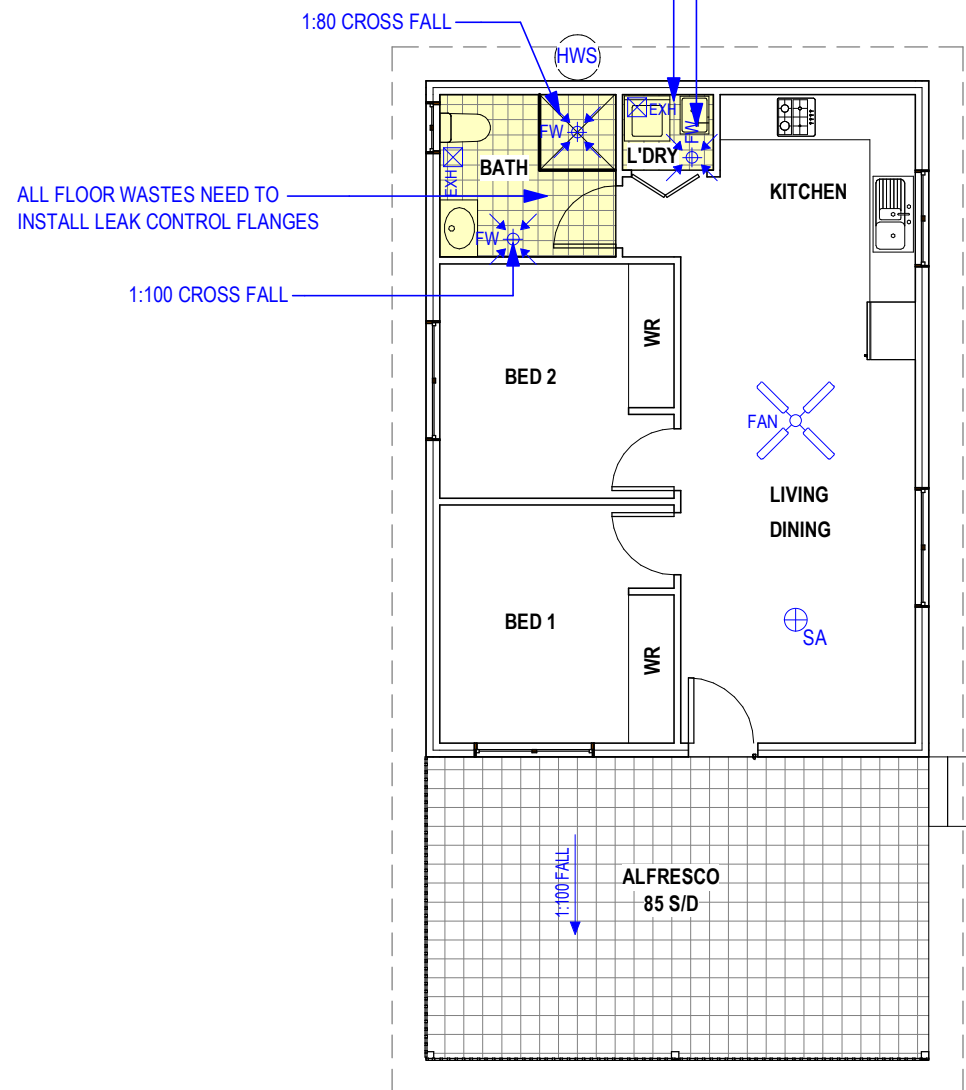

INTERNAL WET AREA DOOR THRESHOLD

WATERPROOFED UNDER SLIDING DOOR &
INSTALLED WATER-STOP ANGLE TO
COMPLIED WITH AS4654.2

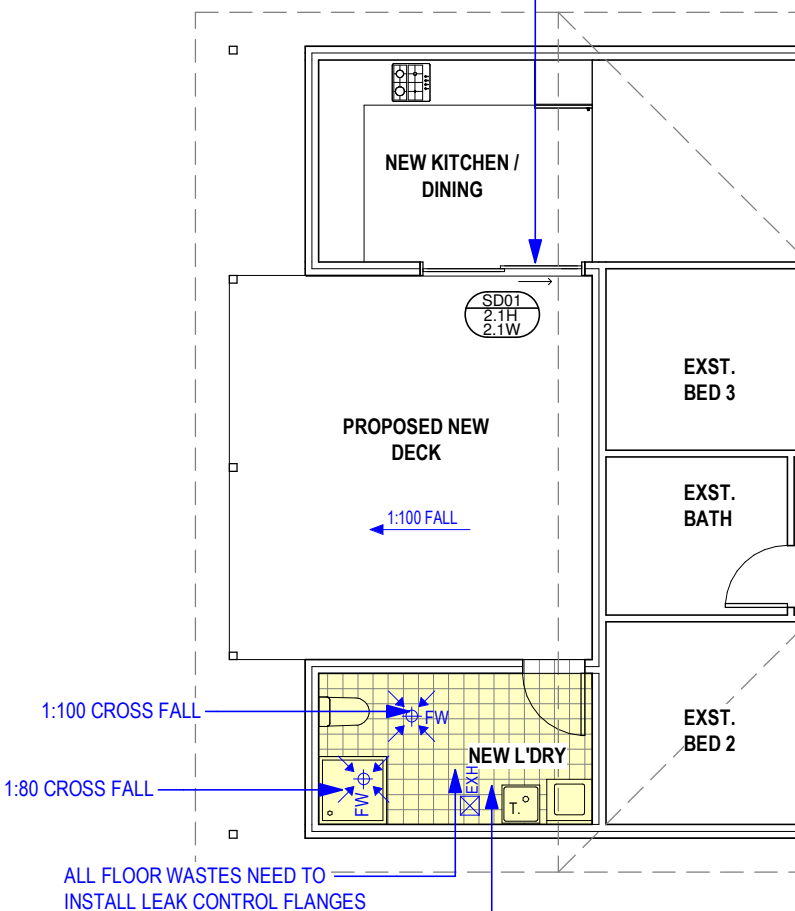

MV DISCHARGE TO EXTERNAL WALL
(MUST REMAIN RUNNING FOR 10
MINUTES AFTER SWITCH IS ON-OFF)

1 WET AREAS PLAN
1 : 100

© THIS DRAWING IS THE PROPERTY OF LT DESIGN & CONSULTING PTY LTD AND WE RESERVE THE COPYRIGHT TO ALL OUR DESIGNS WHICH CANNOT BE REPRODUCED (IN PART OR IN WHOLE) BEFORE FIRST OBTAINING WRITTEN CONSENT. CONTRAVENTION WILL BE PROSECUTED

- FIGURED DIMENSIONS TO BE TAKEN IN PREFERENCE TO SCALE.
- BUILDERS' WORK TO COMPLY WITH THE LATEST BCA AND ITS AMENDMENTS AND RELEVANT AUSTRALIAN STANDARDS REFERRED WITHIN.

No.	Description	Date



bda BUILDING DESIGNERS AUSTRALIA
Accreditation No: 6302
Shop 6A/80 Thorne Rd, Fairfield West
0414 891 998 - Le@LTDesign.net.au

Building Design | 3D Modeling | Drafting | Detailing

DRAWING:
WET AREAS PLAN

CLIENT & PROJECT: LOT 152 IN DP 28393
DEMOLITION OF EXISTING AWNING & GARAGE & PROPOSED SECONDARY DWELLING AND NEW ADDITIONS TO EXIST. HOUSE AT: NO.6 BELLEVUE STREET, BLACKTOWN


COMPLYING DEVELOPMENT CERTIFICATE

DATE:
16/04/2026
DWG NO:
GF-0126-10
SCALE:
1 : 100 (A3)


DRW BY:
LT



NOTES:
ALL WATERPROOFING
MUST BE COMPLIED WITH:
- AS4654.2-2012
- NCC 2022 - VOLUME 2 -
HOUSING PROVISIONS

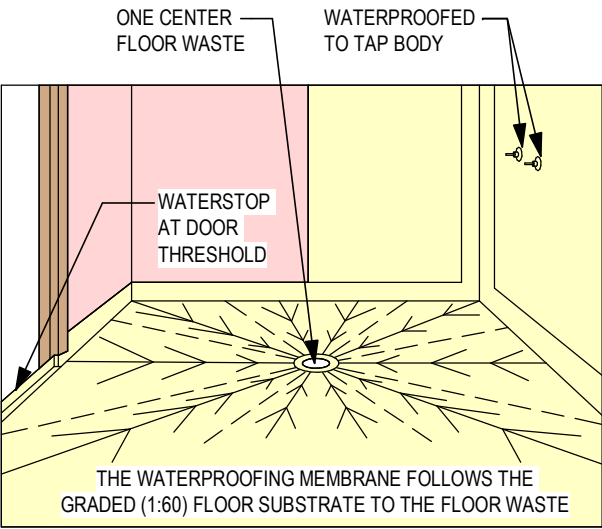

C01 CROSS FALL TO FLOOR WASTE

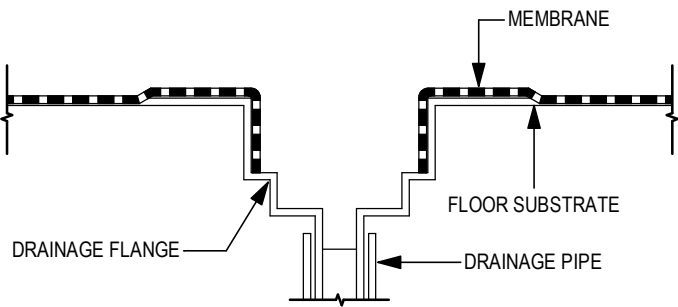


**TYPICAL MEMBRANE TERMINATION
AT DRAINAGE OUTLET**
NOT TO SCALE

C02 LEAK CONTROL FLANGES




**PUDDLE / LEAK CONTROL
DRAINAGE FLANGES**


NOTE: MUST BE APPLIED TO ALL FLOOR WASTES IN WET AREA FOR
GROUND AND UPPER FLOOR / ENTIRE BUILDING
(CLASS 1 BUILDING: CONCRETE FLOOR - MAY SIT ON TOP OF
CONCRETE OR TILE BED FOR - CONCRETE FLOOR ONLY,
OTHER FLOORS - RECESSED INTO FLOOR SUBSTRATE OR TILE BED)

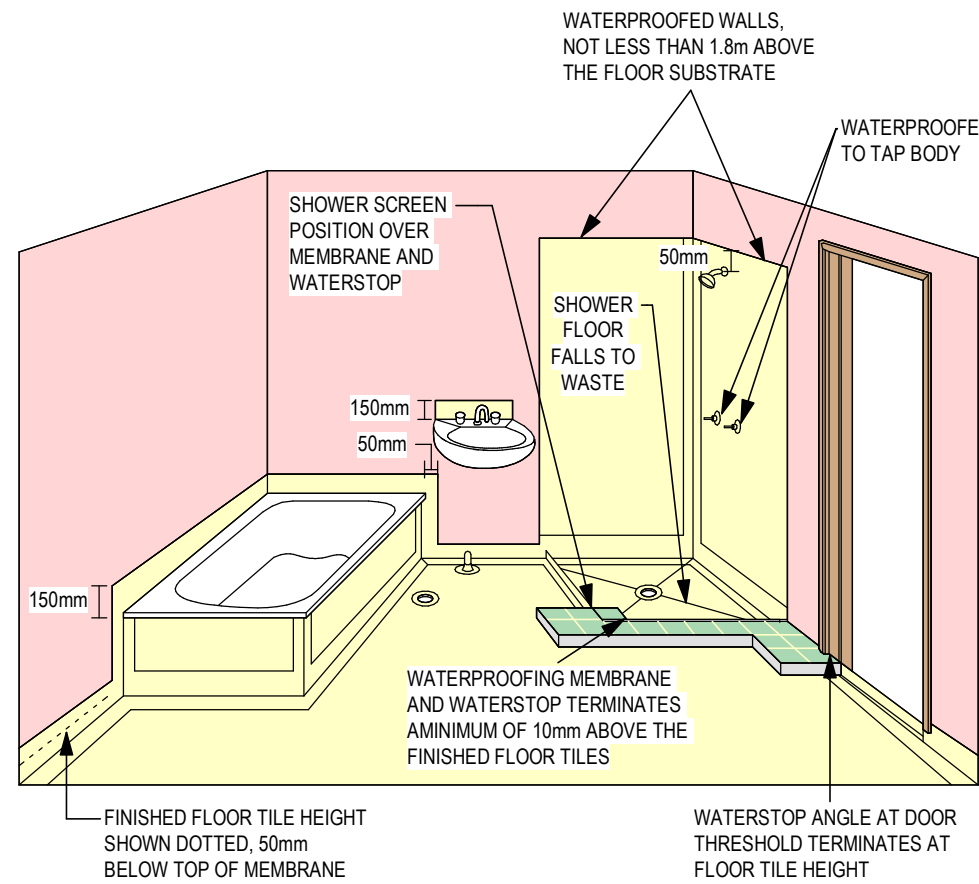

C03 WATERPROOFING DETAILS AROUND BATHROOM

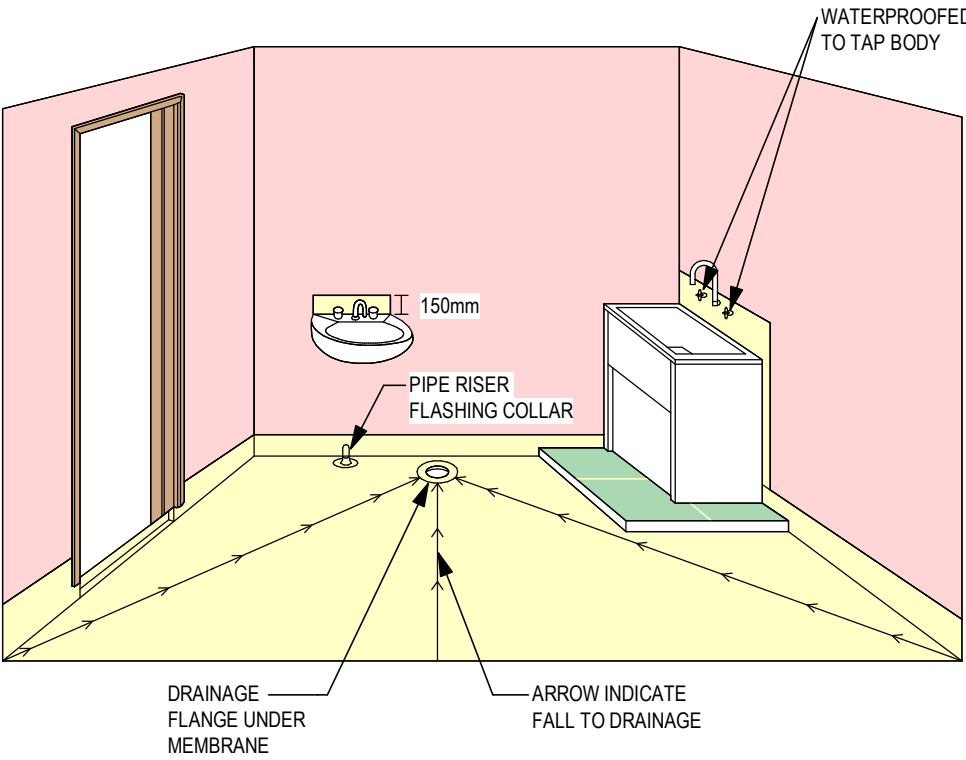

C04 WATERPROOFING DETAILS AROUND LAUNDRY

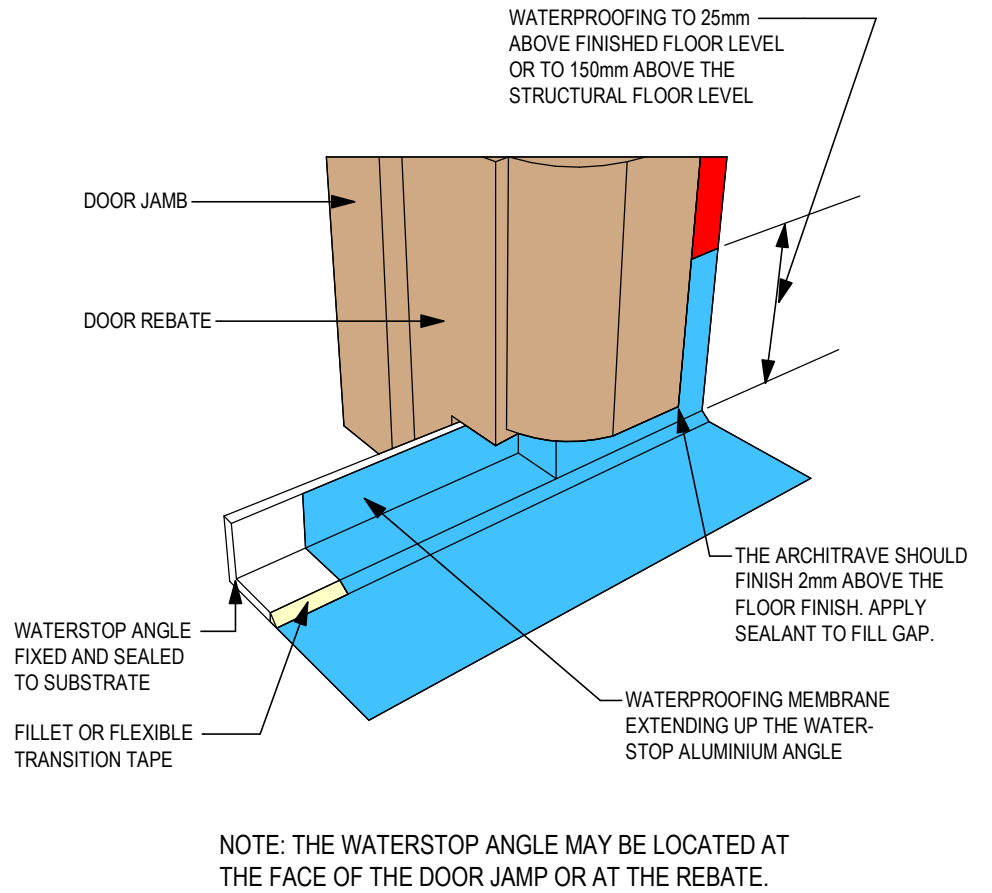

C05 WATERPROOFING UNDER DOOR ARCHITRAVE

© THIS DRAWING IS THE PROPERTY OF LT DESIGN & CONSULTING PTY LTD AND WE RESERVE THE COPYRIGHT TO ALL OUR DESIGNS WHICH CANNOT BE REPRODUCED (IN PART OR IN WHOLE) BEFORE FIRST OBTAINING WRITTEN CONSENT. CONTRAVENTION WILL BE PROSECUTED

- FIGURED DIMENSIONS TO BE TAKEN IN PREFERENCE TO SCALE.
- BUILDERS' WORK TO COMPLY WITH THE LATEST BCA AND ITS AMENDMENTS AND RELEVANT AUSTRALIAN STANDARDS REFERRED WITHIN.

No.	Description	Date



Building Design | 3D Modeling | Drafting | Detailing



Accreditation No: 6302
Shop 6A/80 Thorne Rd, Fairfield West
0414 891 998 - Le@LTDesign.net.au


DRAWING:
TYPICAL WATERPROOFING CONSTRUCTION DETAILS

CLIENT & PROJECT: LOT 152 IN DP 28393
**DEMOLITION OF EXISTING AWNING & GARAGE & PROPOSED
SECONDARY DWELLING AND NEW ADDITIONS TO EXIST. HOUSE
AT: NO.6 BELLEVUE STREET, BLACKTOWN**

COMPLYING DEVELOPMENT CERTIFICATE

DATE:
16/04/2026
DWG NO:
GF-0126-11

SCALE:

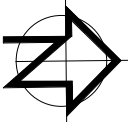

DRW BY:
LT

1 : 5 (A3)