
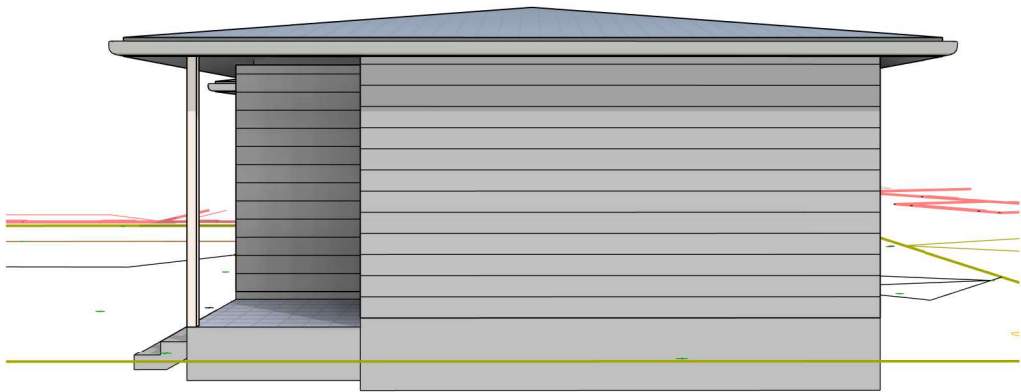
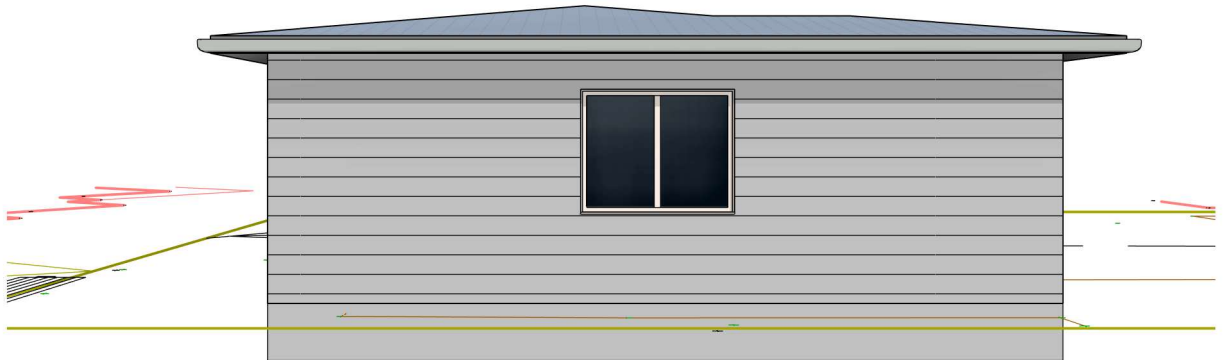


PROPOSED SECONDARY DWELLING WITH
ATTACHED GARAGE
AT: NO.8 IONA STREET, BLACKTOWN, NSW 2148

SHEET LIST	
SHEET NUMBER	SHEET NAME
GF-1126-00	3D VIEWS
GF-1126-01	SITE/ROOF PLAN
GF-1126-02	PROPOSED FLOOR PLAN
GF-1126-03	ELEVATIONS
GF-1126-04	SECTIONS
GF-1126-05	EROSION & SEDIMENT CONTROL PLAN
GF-1126-06	BASIX COMMITMENTS PLAN
GF-1126-07	WET AREAS PLAN
GF-1126-08	TYPICAL WATERPROOFING CONSTRUCTION DETAILS
GF-1126-09	FIREWALL DETAILS - 16MM FYRCHEK SYSTEM

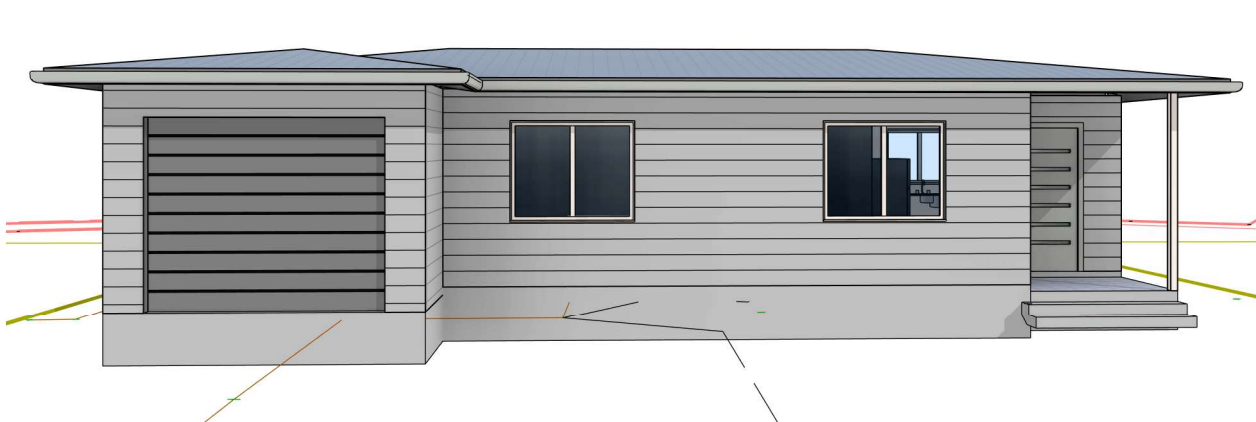

© THIS DRAWING IS THE PROPERTY OF LT DESIGN & CONSULTING PTY LTD AND WE RESERVE THE COPYRIGHT TO ALL OUR DESIGNS WHICH CANNOT BE REPRODUCED (IN PART OR IN WHOLE) BEFORE FIRST OBTAINING WRITTEN CONSENT. CONTRAVENTION WILL BE PROSECUTED

- FIGURED DIMENSIONS TO BE TAKEN IN PREFERENCE TO SCALE.
- BUILDERS' WORK TO COMPLY WITH THE LATEST BCA AND ITS AMENDMENTS AND RELEVANT AUSTRALIAN STANDARDS REFERRED WITHIN.

No.	Description	Date



Building Design | 3D Modeling | Drafting | Detailing



BUILDING DESIGNERS AUSTRALIA
Accreditation No: 6302
Shop 6A/80 Thorne Rd, Fairfield West
0414 891 998 - Le@LTDesign.net.au

DRAWING: 3D VIEWS			
CLIENT & PROJECT: LOT 288 IN DP 25318			DATE: 14/07/2026
PROPOSED SECONDARY DWELLING WITH ATTACHED GARAGE AT: NO.8 IONA STREET, BLACKTOWN, NSW 2148			DWG NO: GF-1126-00
COMPLYING DEVELOPMENT CERTIFICATE			SCALE:

SITE CALCULATIONS - SEPP 2021				
SITE AREA: 608.4 SQM	EXISTING	PROPOSED	REQUIRED	COMPLY
EXISTING GROUND FLOOR	103.5 sqm			
PROPOSED SECONDARY DWELLING		60 sqm	60 sqm (Max.)	YES
PROPOSED GARAGE		29 sqm		
TOTAL FLOOR AREA	192.5 sqm		380 sqm (Max.)	YES
PRIVATE OPEN SPACE	24.1 sqm		MORE THAN 24 SQM	YES
LANDSCAPE AREA	211.15 sqm (34.70%)		25% (Min.)	YES
SITE COVERAGE	192.5 sqm (31.64%)		50% (Max.)	YES

NOTES:

1. CHECK DIMENSIONS ON SITE BEFORE PROCEEDING WITH THE WORK OF THE CONTRACT. NOTIFY BUILDING DESIGNER OF OMISSIONS OR CONFLICT IN DRAWINGS OR SPECIFICATIONS.


2. FIGURED DIMENSIONS ARE TO BE TAKEN IN PREFERENCE TO SCALE. DO NOT SCALE OFF DRAWINGS.

3. ALL CONSTRUCTION WORK IS TO COMPLY WITH RELEVANT AUSTRALIAN STANDARDS AND THE NCC.

4. REFER TO ACCOMPANYING BASIX CERTIFICATE REFERENCED FOR COMMITMENTS FOR THIS DEVELOPMENT.

5. **SA:** SMOKE ALARM
SMOKE ALARMS TO BE INSTALLED IN ACCORDANCE WITH AS 3786-2014 & CONNECTED TO MAINS POWER

WINDOW SCHEDULE		
Mark	Width	Height
W1	1500	1200
W2	1500	1200
W3	1500	1200
W4	1500	1200
W5	600	900
W6	1200	920

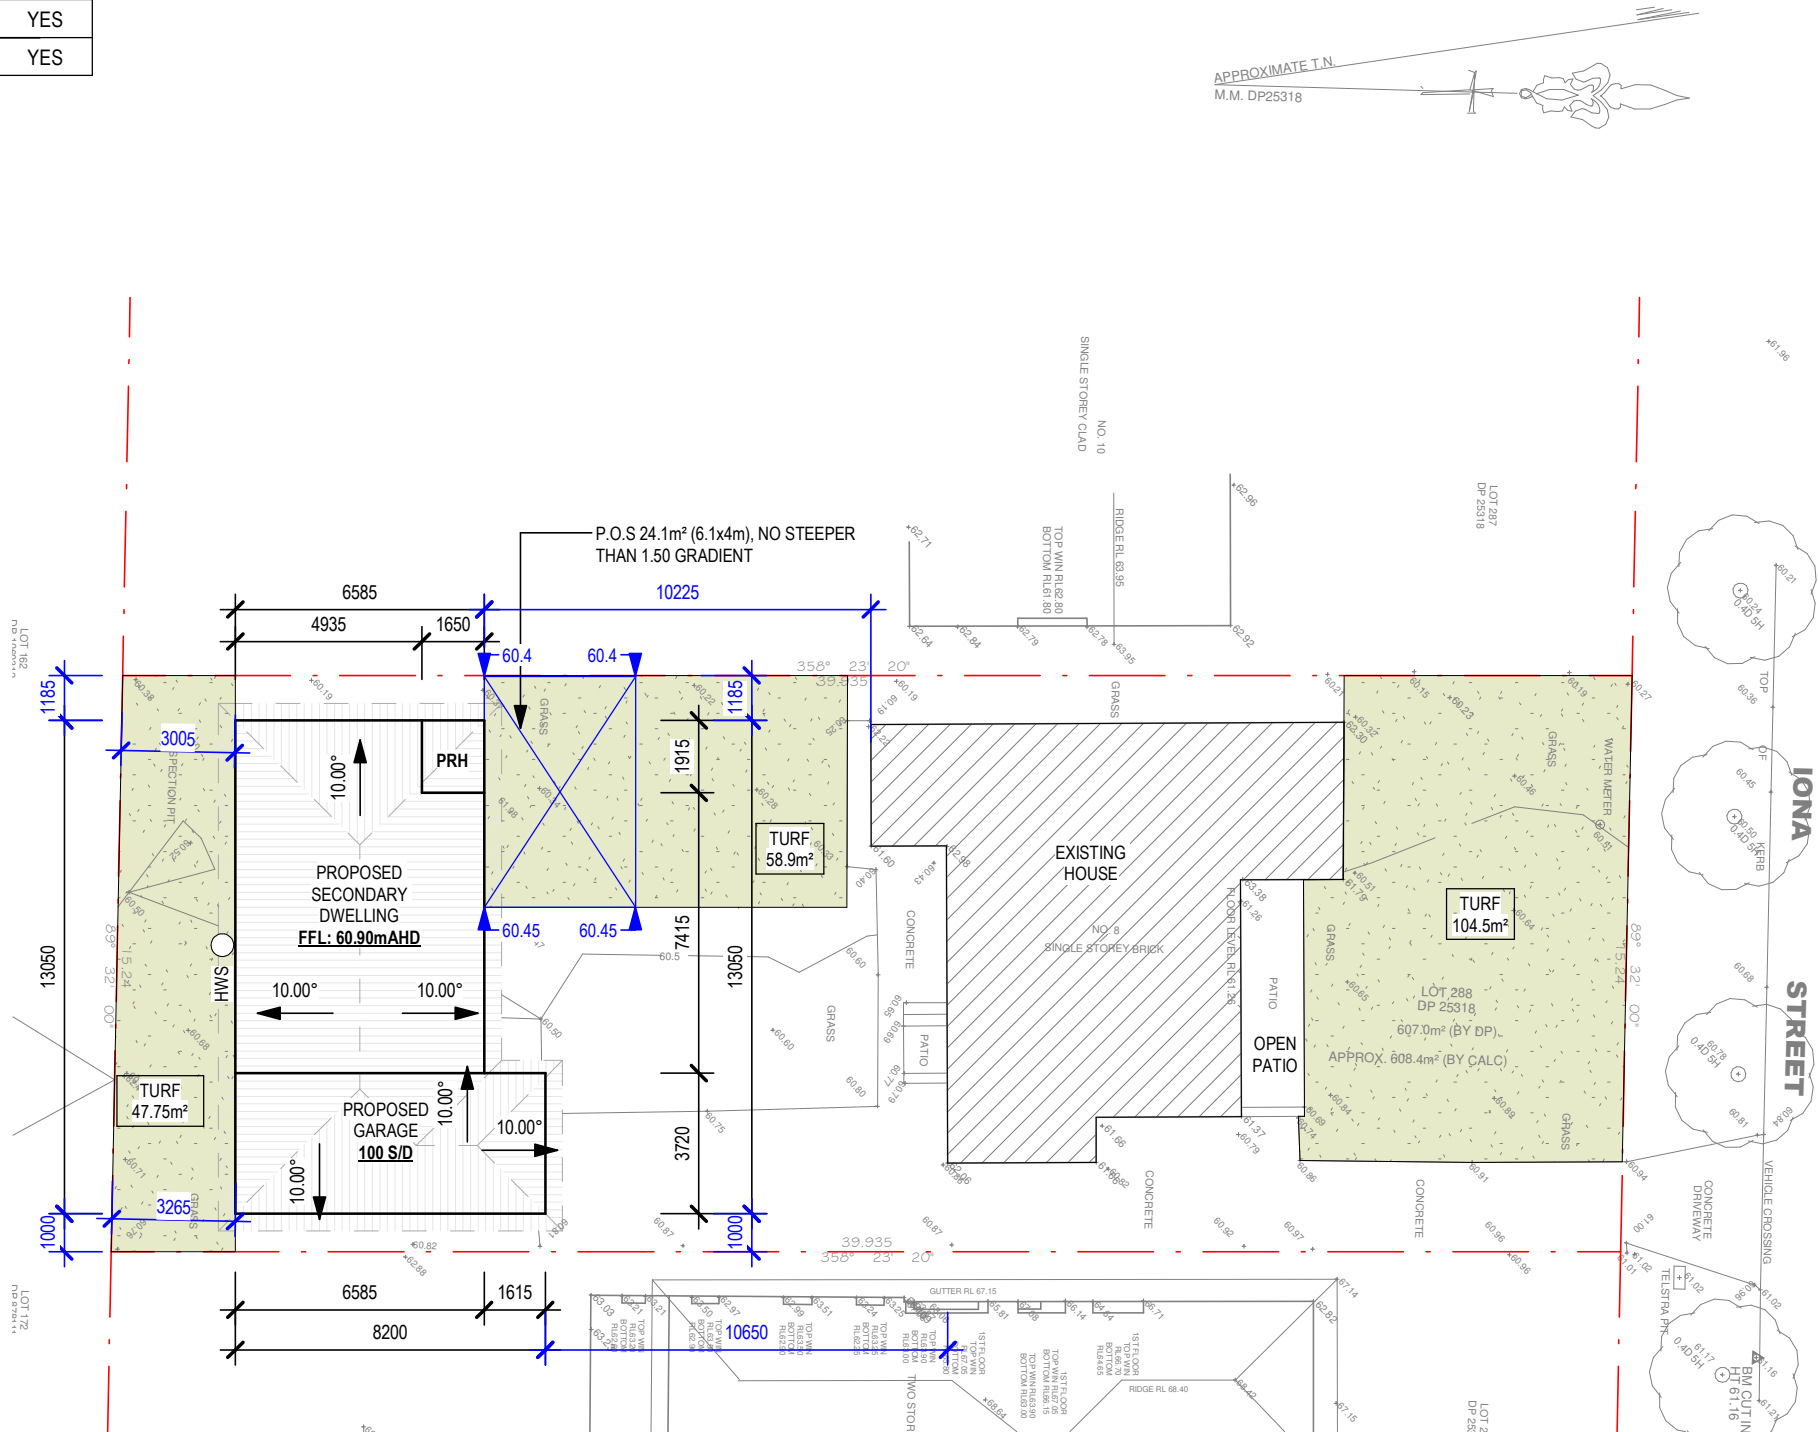

1 SITE & ROOF PLAN
1 : 200

© THIS DRAWING IS THE PROPERTY OF LT DESIGN & CONSULTING PTY LTD AND WE RESERVE THE COPYRIGHT TO ALL OUR DESIGNS WHICH CANNOT BE REPRODUCED (IN PART OR IN WHOLE) BEFORE FIRST OBTAINING WRITTEN CONSENT. CONTRAVENTION WILL BE PROSECUTED

- FIGURED DIMENSIONS TO BE TAKEN IN PREFERENCE TO SCALE.
- BUILDERS' WORK TO COMPLY WITH THE LATEST BCA AND ITS AMENDMENTS AND RELEVANT AUSTRALIAN STANDARDS REFERRED WITHIN.

No.	Description	Date



Building Design | 3D Modeling | Drafting | Detailing



BUILDING DESIGNERS AUSTRALIA

Accreditation No: 6302
Shop 6A/80 Thorney Rd, Fairfield West
0414 891 998 - Le@LTDesign.net.au

DRAWING: SITE/ROOF PLAN			
CLIENT & PROJECT: LOT 288 IN DP 25318			DATE: 14/07/2026
PROPOSED SECONDARY DWELLING WITH ATTACHED GARAGE AT: NO.8 IONA STREET, BLACKTOWN, NSW 2148		DWG NO: GF-1126-01	DRW BY: LT
COMPLYING DEVELOPMENT CERTIFICATE		SCALE:	As indicated (A3)

VJ : VERTICAL BRICK JOINTS


WH : WEEPHOLES

LOH : LIFT OFF HINGES DOOR TO COMPLY WITH NCC 2022

SA : SMOKE ALARM TO COMPLY WITH AS.3786

FW : FLOOR WASTE

EXH : MECHANICAL VENTILATION SYSTEM - DISCHARGING TO EXTERNAL WALL FOR 10 MINUTES AFTER LIGHT SWITCHES OFF IN ACCORDANCE WITH PART 10.8 OF NCC 2002

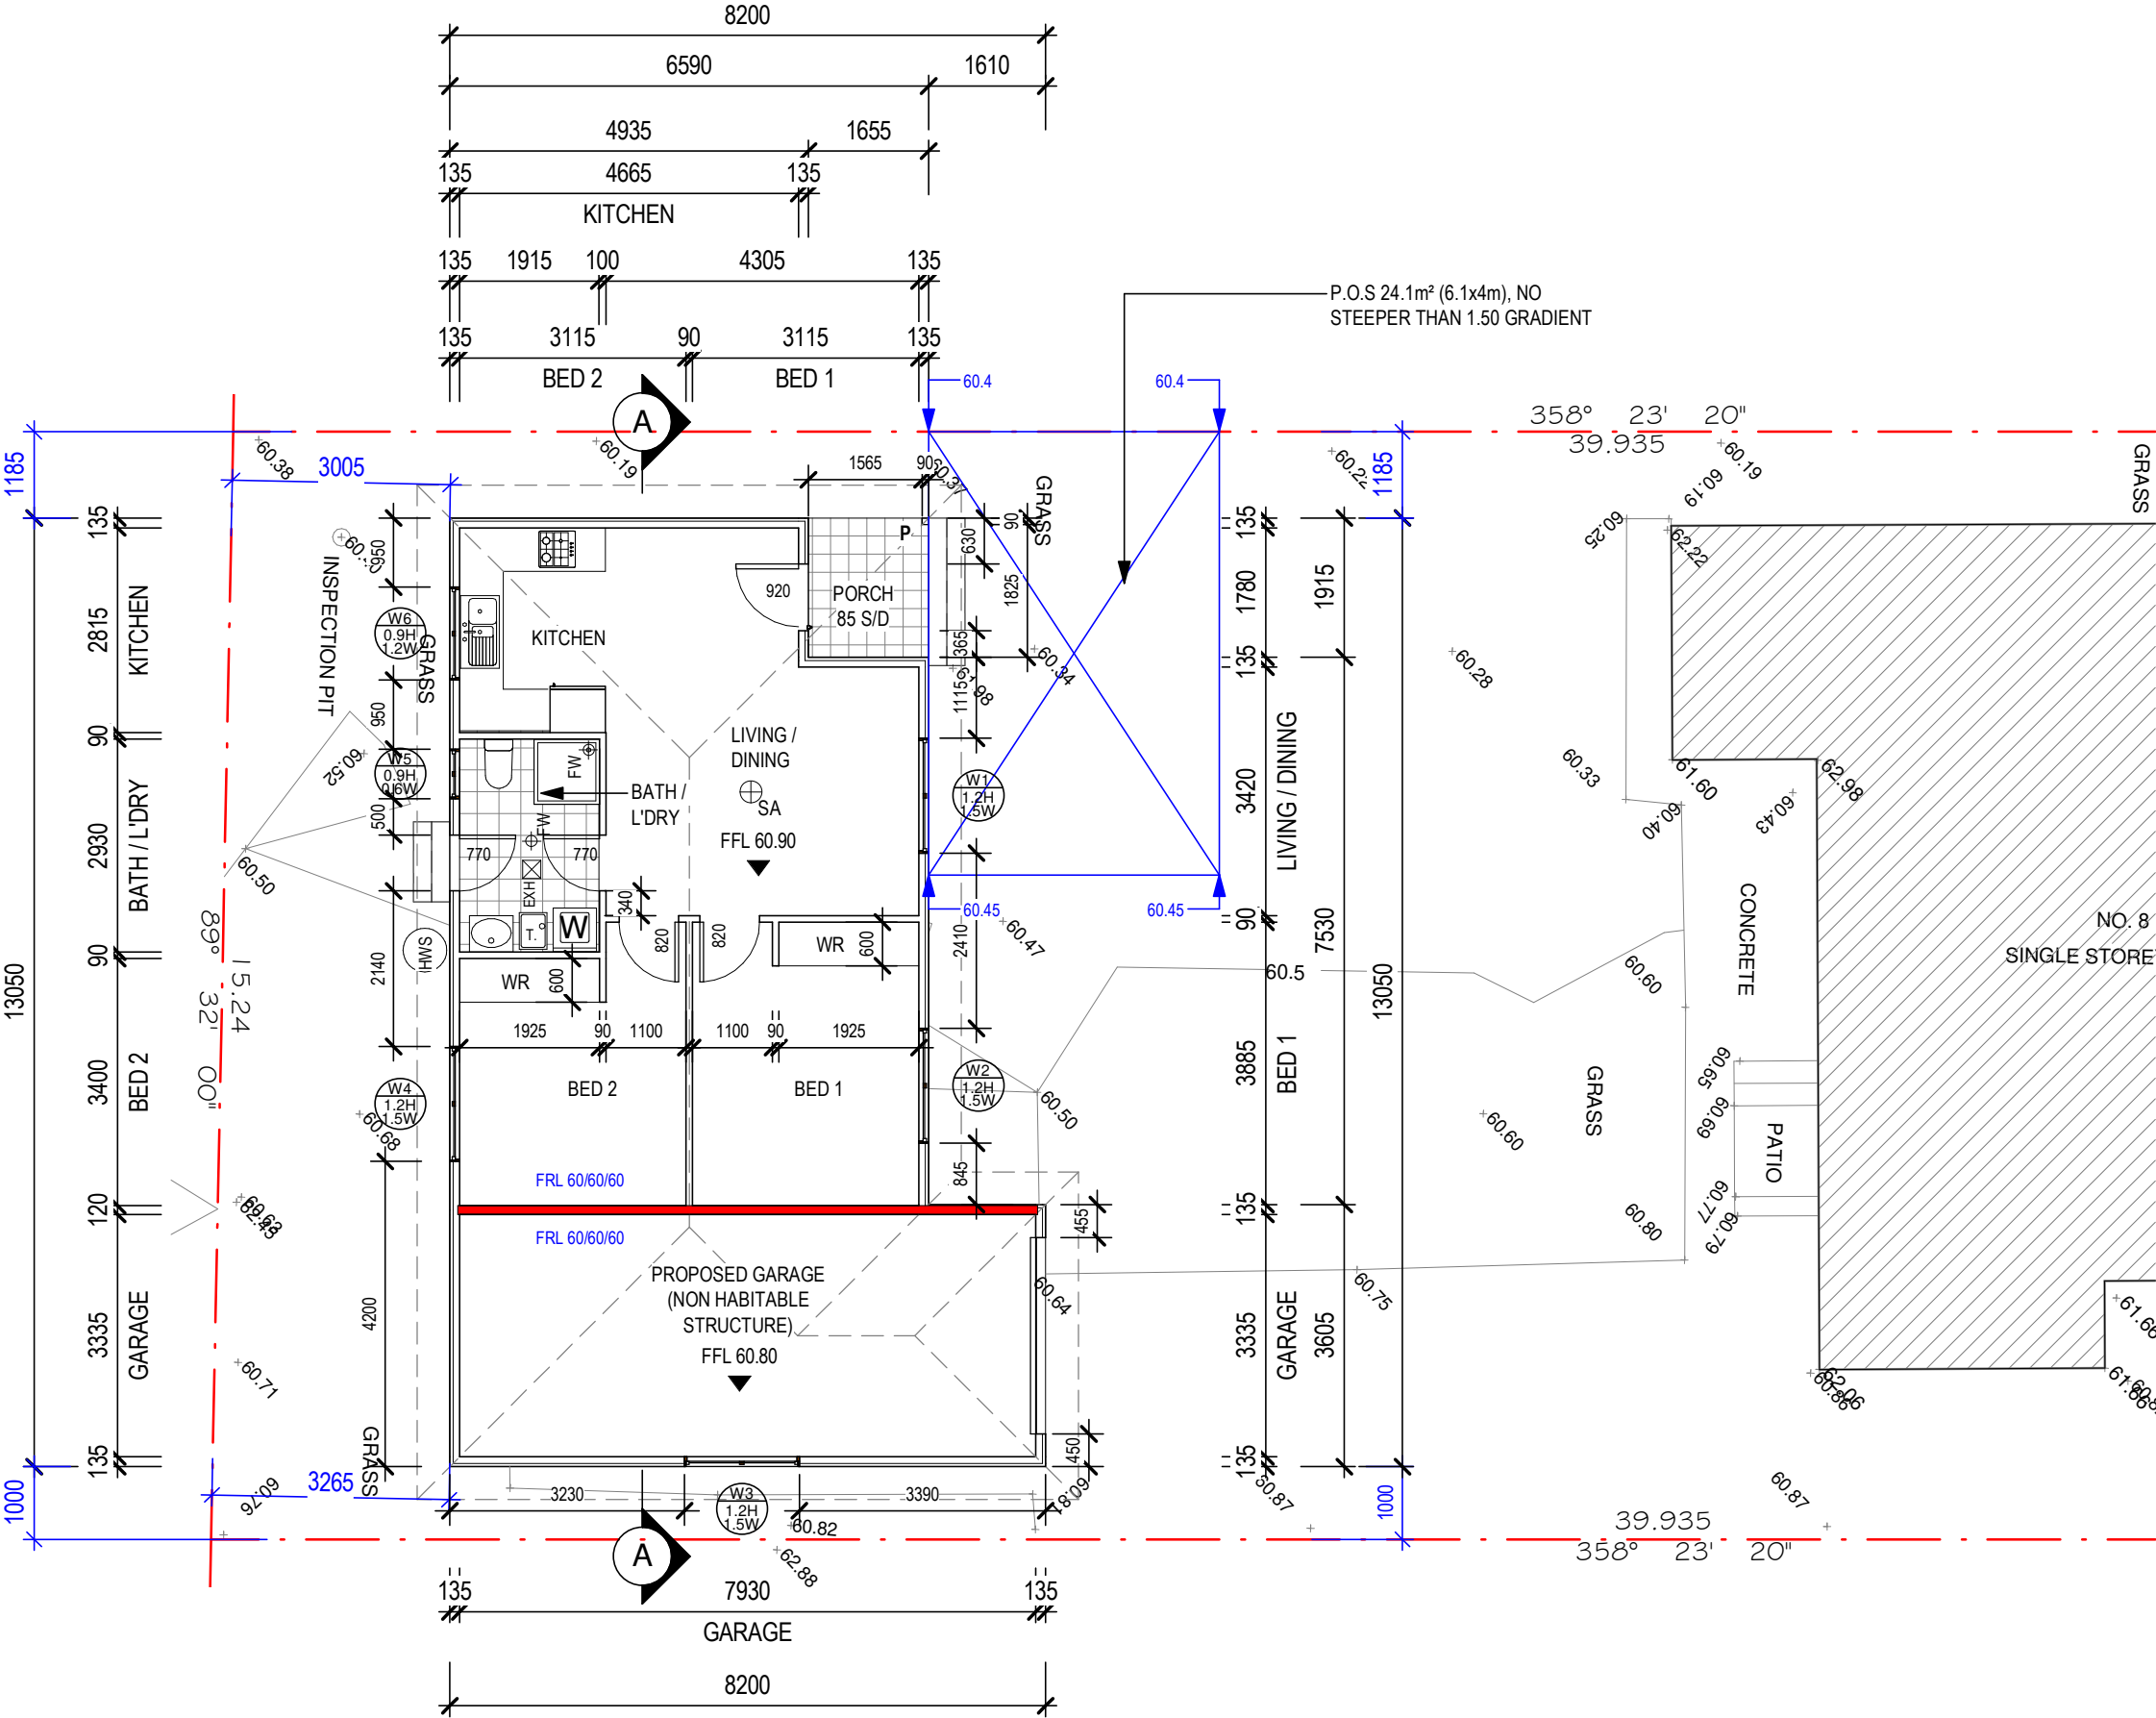

1 PROPOSED GROUND FLOOR PLAN
1 : 100

© THIS DRAWING IS THE PROPERTY OF LT DESIGN & CONSULTING PTY LTD AND WE RESERVE THE COPYRIGHT TO ALL OUR DESIGNS WHICH CANNOT BE REPRODUCED (IN PART OR IN WHOLE) BEFORE FIRST OBTAINING WRITTEN CONSENT. CONTRAVENTION WILL BE PROSECUTED

FIGURED DIMENSIONS TO BE TAKEN IN PREFERENCE TO SCALE.

BUILDERS' WORK TO COMPLY WITH THE LATEST BCA AND ITS AMENDMENTS AND RELEVANT AUSTRALIAN STANDARDS REFERRED WITHIN.

No.	Description	Date



Building Design | 3D Modeling | Drafting | Detailing



Accreditation No: 6302
Shop 6A/80 Thorney Rd, Fairfield West
0414 891 998 - Le@LTDesign.net.au

DRAWING:
PROPOSED FLOOR PLAN

CLIENT & PROJECT: LOT 288 IN DP 25318

PROPOSED SECONDARY DWELLING WITH ATTACHED GARAGE
AT: NO.8 IONA STREET, BLACKTOWN, NSW 2148

COMPLYING DEVELOPMENT CERTIFICATE

DATE:
14/07/2026
DWG NO:
GF-1126-02


SCALE:




DRW BY:
LT

1 : 100 (A3)


- VJ : VERTICAL BRICK JOINTS
- WH : WEEPHOLES
- LOH : LIFT OFF HINGES DOOR TO COMPLY WITH NCC 2022
- ⊕ SA : SMOKE ALARM TO COMPLY WITH AS.3786
- ⊕ FW : FLOOR WASTE
- ⊠ EXH : MECHANICAL VENTILATION SYSTEM - DISCHARGING TO EXTERNAL WALL FOR 10 MINUTES AFTER LIGHT SWITCHES OFF IN ACCORDANCE WITH PART 10.8 OF NCC 2002

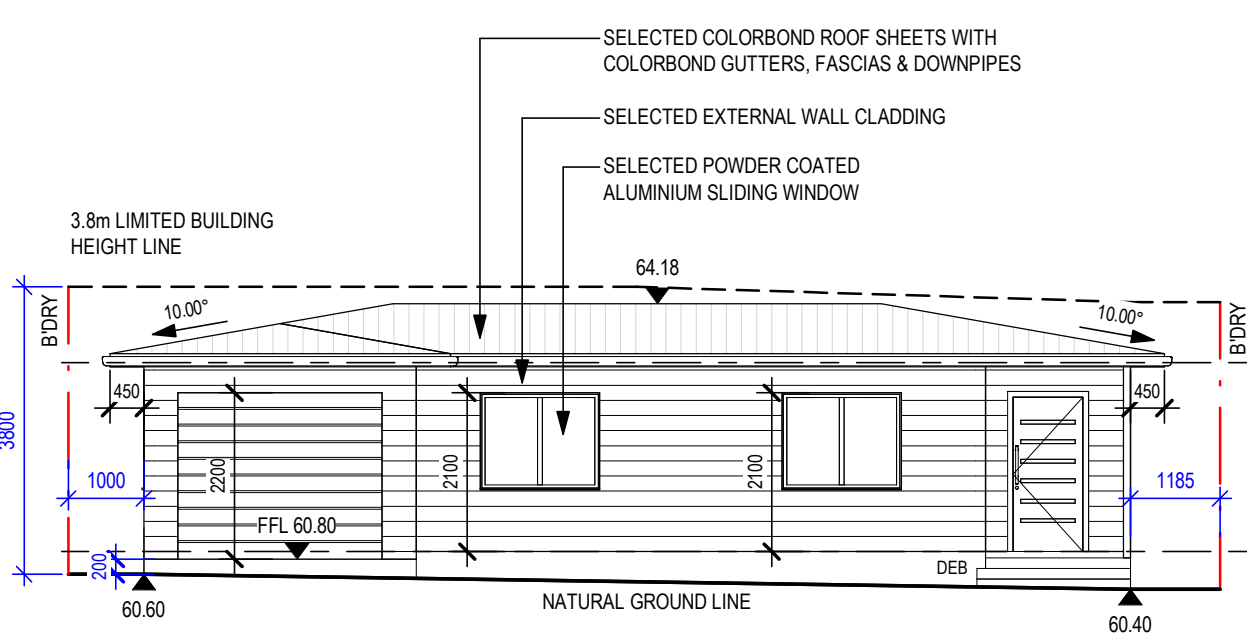


1 NORTH ELEVATION
1 : 100

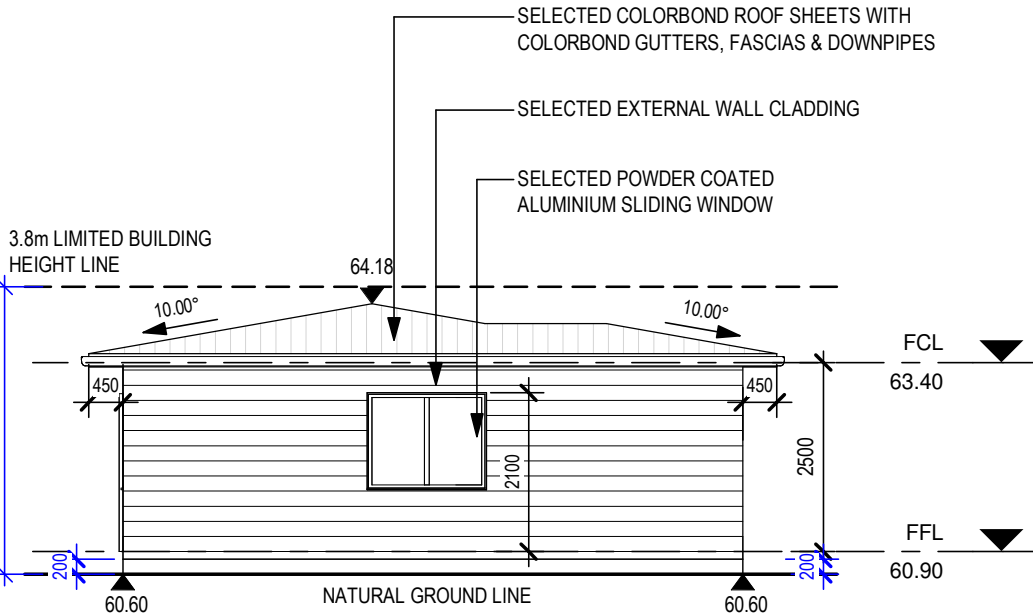

3 EAST ELEVATION
1 : 100

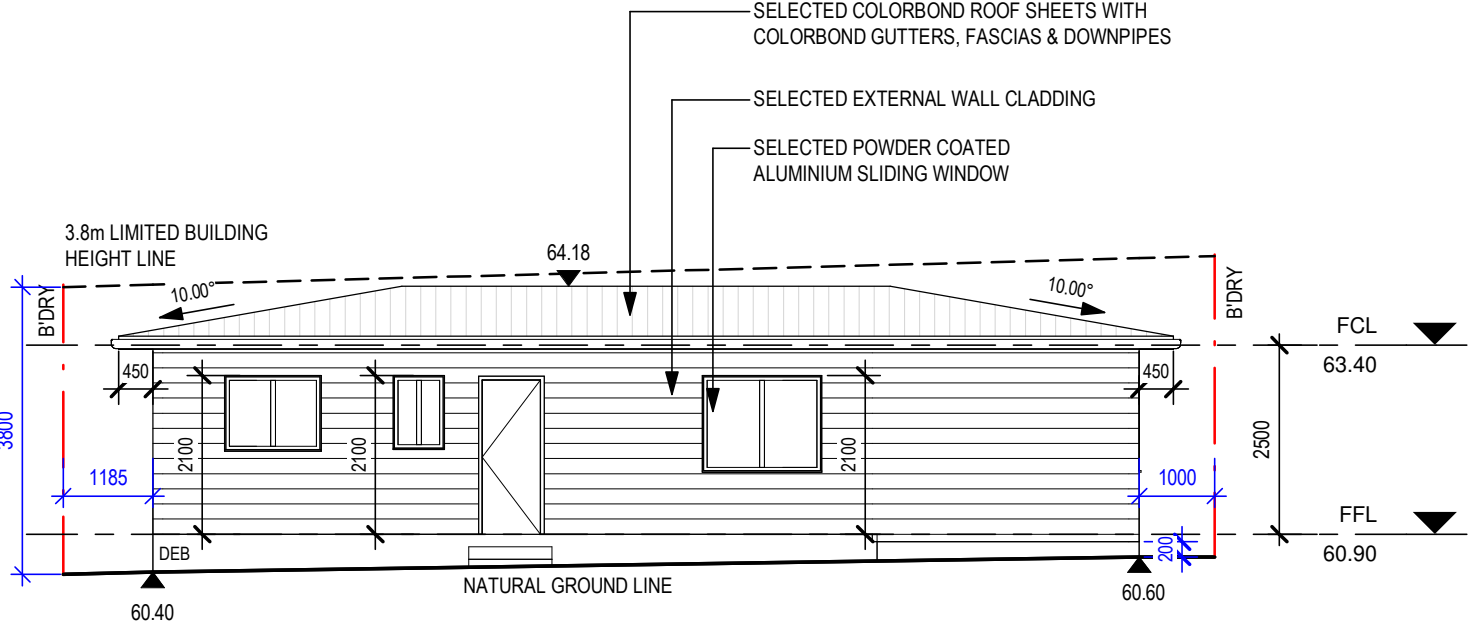

2 SOUTH ELEVATION
1 : 100

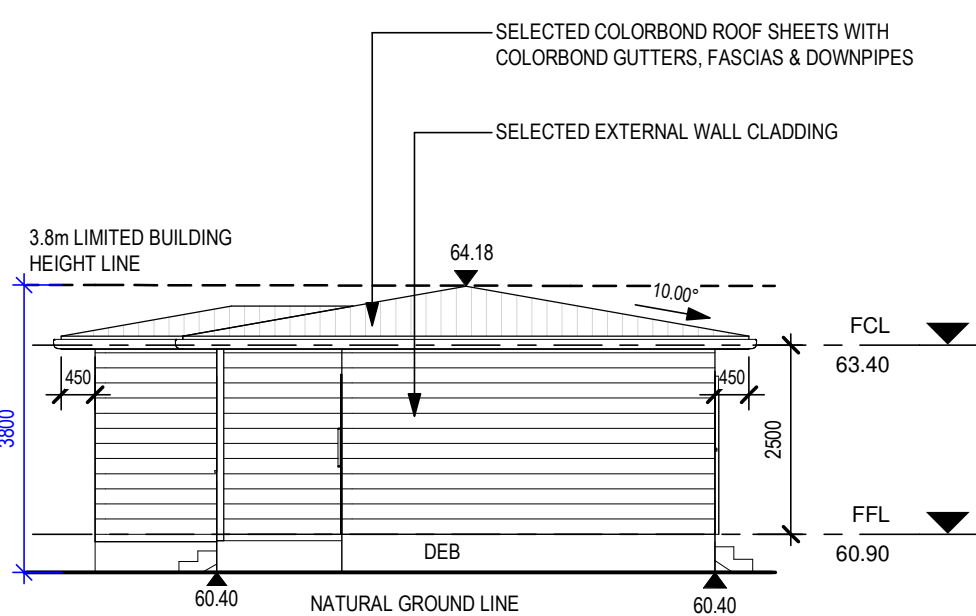

4 WEST ELEVATION
1 : 100

NOTED: WEEPHOLES TO BE INSTALLED AS PER NCC, AS 3700, AS 1773 AND OTHER RELEVANT AUSTRALIAN STANDARDS WITH IN 1.2m

NOTE: EAVES ENCROACHING WITHIN 900mm OF AN ALLOTMENT BOUNDARY AND 1800mm FROM ANOTHER BUILDING TO BE NON-COMBUSTILE

AC UNITS/HOT WATER UNITS/RWTS TO BE MINIMUM 450MM FROM BDY AND 900MM FROM ANOTHER BUILDING

© THIS DRAWING IS THE PROPERTY OF LT DESIGN & CONSULTING PTY LTD AND WE RESERVE THE COPYRIGHT TO ALL OUR DESIGNS WHICH CANNOT BE REPRODUCED (IN PART OR IN WHOLE) BEFORE FIRST OBTAINING WRITTEN CONSENT. CONTRAVENTION WILL BE PROSECUTED

• FIGURED DIMENSIONS TO BE TAKEN IN PREFERENCE TO SCALE.

• BUILDERS' WORK TO COMPLY WITH THE LATEST BCA AND ITS AMENDMENTS AND RELEVANT AUSTRALIAN STANDARDS REFERRED WITHIN.

No.	Description	Date



Building Design | 3D Modeling | Drafting | Detailing



BUILDING
DESIGNERS
AUSTRALIA

Accreditation No: 6302
Shop 6A/80 Thorney Rd, Fairfield West
0414 891 998 - Le@LTDesign.net.au

DRAWING:
ELEVATIONS

CLIENT & PROJECT: LOT 288 IN DP 25318

**PROPOSED SECONDARY DWELLING WITH ATTACHED GARAGE
AT: NO.8 IONA STREET, BLACKTOWN, NSW 2148**


COMPLYING DEVELOPMENT CERTIFICATE

DATE:
14/07/2026
DWG NO:
GF-1126-03


DRW BY:
LT

SCALE: 1 : 100 (A3)



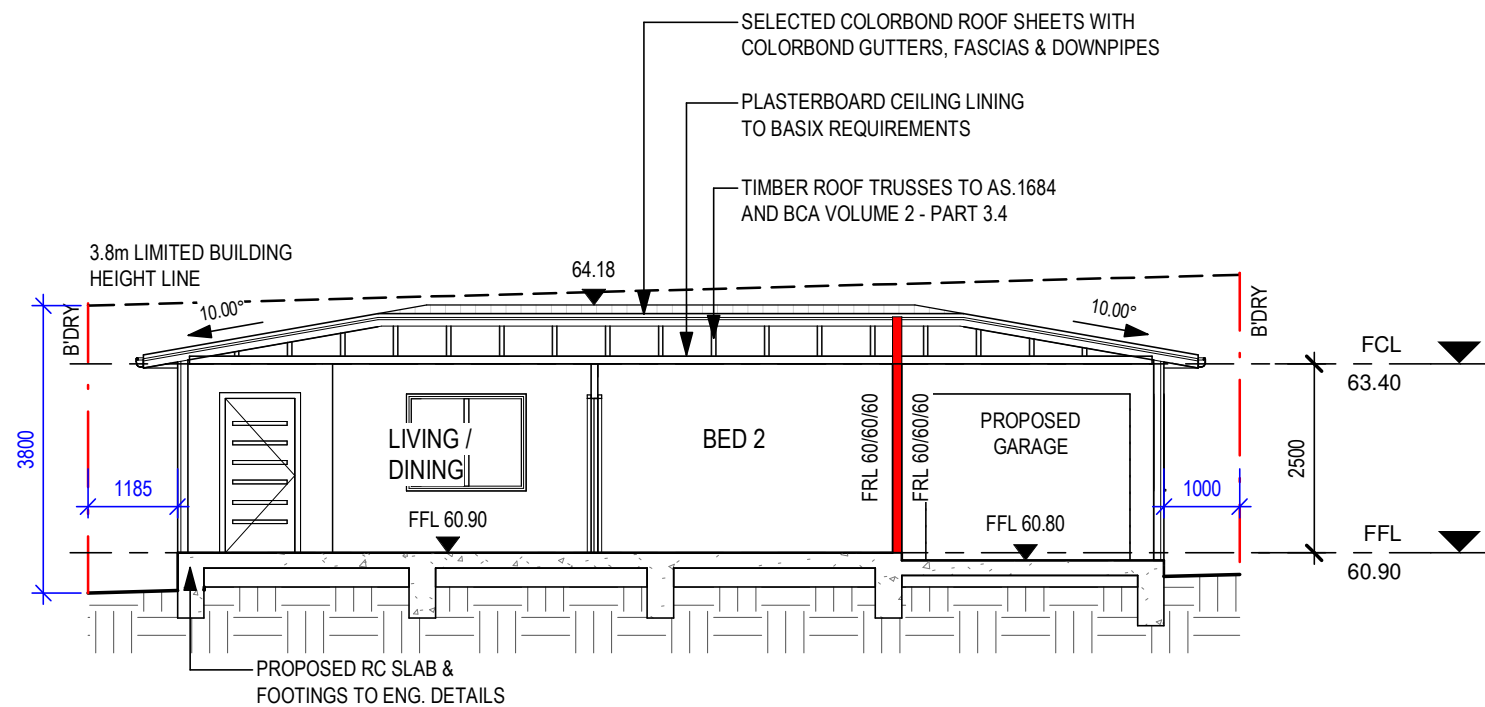

1 SECTION A-A
1 : 100

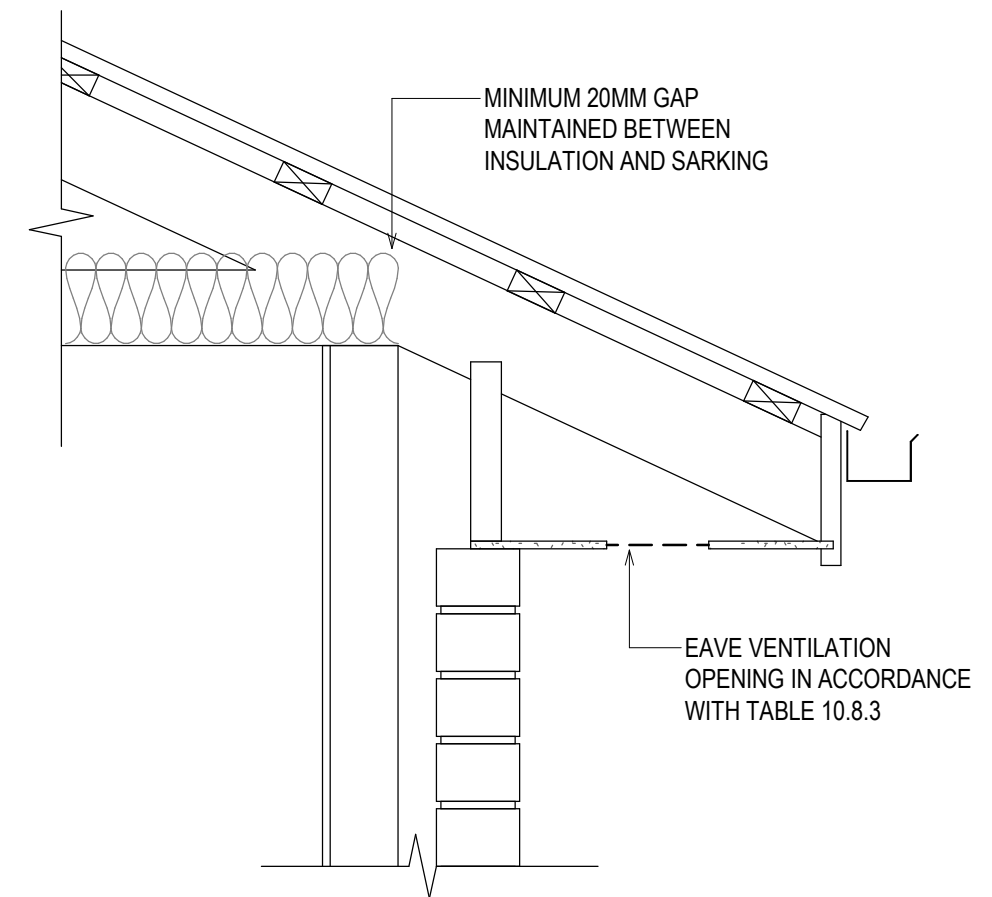

CONDENSATION MANAGEMENT DETAILS

CONDENSATION MANAGEMENT

- (1) AN EXHAUST SYSTEM INSTALLED IN A KITCHEN, BATHROOM, SANITARY COMPARTMENT OR LAUNDRY MUST HAVE A MINIMUM FLOW RATE OF—
- (A) 25 L/S FOR A BATHROOM OR SANITARY COMPARTMENT; AND
 - (B) 40 L/S FOR A KITCHEN OR LAUNDRY.
- (2) EXHAUST FROM A KITCHEN, KITCHEN RANGE HOOD, BATHROOM, SANITARY COMPARTMENT OR LAUNDRY MUST DISCHARGE DIRECTLY OR VIA A SHAFT OR DUCT TO OUTDOOR AIR.
- (3) WHERE A VENTING CLOTHES DRYER IS INSTALLED, IT MUST DISCHARGE DIRECTLY OR VIA A SHAFT OR DUCT TO OUTDOOR AIR.
- (4) AN EXHAUST SYSTEM THAT IS NOT RUN CONTINUOUSLY AND IS SERVING A BATHROOM OR SANITARY COMPARTMENT THAT IS NOT VENTILATED IN ACCORDANCE WITH 10.6.2(A) MUST—
- (A) BE INTERLOCKED WITH THE ROOM'S LIGHT SWITCH; AND
 - (B) INCLUDE A RUN-ON TIMER SO THAT THE EXHAUST SYSTEM CONTINUES TO OPERATE FOR 10 MINUTES AFTER THE LIGHT SWITCH IS TURNED OFF.
- (5) EXCEPT FOR ROOMS THAT ARE VENTILATED IN ACCORDANCE WITH 10.6.2(A), A ROOM WITH AN EXHAUST SYSTEM IN ACCORDANCE WITH (1) MUST BE PROVIDED WITH MAKE-UP AIR—
- (A) VIA OPENINGS TO AN ADJACENT ROOM WITH A FREE AREA OF 14,000 MM²; OR IN ACCORDANCE WITH AS 1668.2.

NOTE:

EAVES ENCROACHING WITHIN 900mm OF AN ALLOTMENT BOUNDARY AND 1800mm FROM ANOTHER BUILDING TO BE NON-COMBUSTILE

AC UNITS/HOT WATER UNITS/RWTS TO BE MINIMUM 450MM FROM BDY AND 900MM FROM ANOTHER BUILDING

© THIS DRAWING IS THE PROPERTY OF LT DESIGN & CONSULTING PTY LTD AND WE RESERVE THE COPYRIGHT TO ALL OUR DESIGNS WHICH CANNOT BE REPRODUCED (IN PART OR IN WHOLE) BEFORE FIRST OBTAINING WRITTEN CONSENT. CONTRAVENTION WILL BE PROSECUTED

• FIGURED DIMENSIONS TO BE TAKEN IN PREFERENCE TO SCALE.

• BUILDERS' WORK TO COMPLY WITH THE LATEST BCA AND ITS AMENDMENTS AND RELEVANT AUSTRALIAN STANDARDS REFERRED WITHIN.

No.	Description	Date



Building Design | 3D Modeling | Drafting | Detailing



BUILDING
DESIGNERS
AUSTRALIA

Accreditation No: 6302
Shop 6A/80 Thorney Rd, Fairfield West
0414 891 998 - Le@LTDesign.net.au

DRAWING: SECTIONS

CLIENT & PROJECT: LOT 288 IN DP 25318

**PROPOSED SECONDARY DWELLING WITH ATTACHED GARAGE
AT: NO.8 IONA STREET, BLACKTOWN, NSW 2148**

COMPLYING DEVELOPMENT CERTIFICATE

DATE:
14/07/2026

DWG NO:
GF-1126-04

SCALE: As indicated (A3)






DRW BY:
LT

1. NO VEHICLE CROSSING OR STOCKPIILING OF MATERIAL SHOULD OCCUR ON THE VEGETATED BUFFER.
2. ALL SEDIMENT CONTROL STRUCTURES SHOULD BE INSPECTED & MAINTAINED BY THE SITE MANAGE DAILY
3. ALL SEDIMENT RETAINING STRUCTURES SHOULD BE CLEANED ON REACHING 50% STORAGE CAPACITY. SEDIMENT REMOVED SHOULD BE SPREAD WITHIN THE DISTURBED AREA.
4. ALL EXISTING VEGETATION ON THE SITE PERIMETER MUST BE RETAINED.
5. ROOF GUTTERS AND DOWNPIPES MUST BE CONNECT TO THE SITE DRAINAGE IMMEDIATELY AFTER ROOF CONSTRUCTION.
6. ALL DISTURBED AREA ARE TO BE RE-VEGETATED OR STABILISED TO PREVENT EROSION. I.E. LANDSCAPING/ MULCHING/ TURFING.
7. MATERIALS AREA NOT TO BE STORED ON THE FOOTPATH.



SILT FENCE	
STOCKPILE	
MATERIAL STORAGE	
WASTE STORAGE & RECYCLING AREA	
GARBAGE BIN	
ONSITE TOILET	
ACCESS FOR VEHICLES	

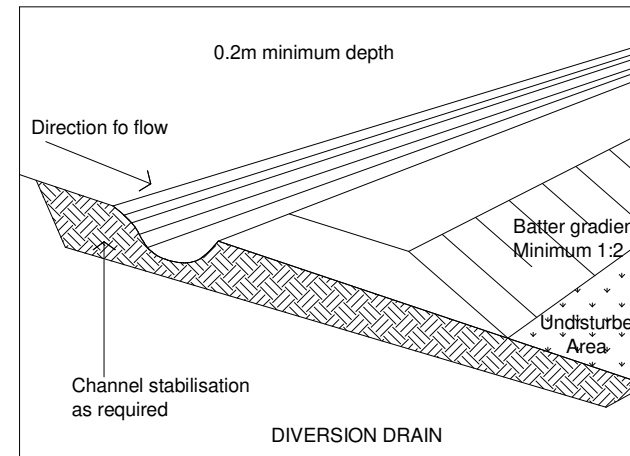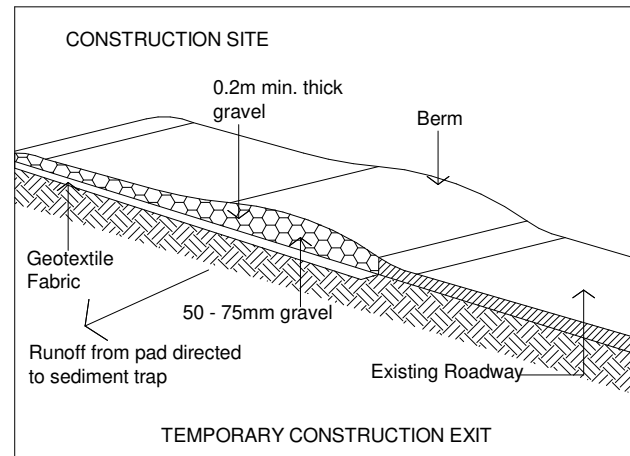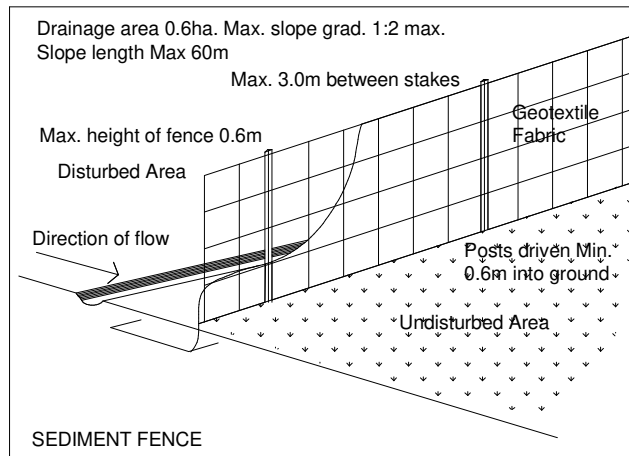

- FIGURED DIMENSIONS TO BE TAKEN IN PREFERENCE TO SCALE.
- BUILDERS' WORK TO COMPLY WITH THE LATEST BCA AND ITS AMENDMENTS AND RELEVANT AUSTRALIAN STANDARDS REFERRED WITHIN.

[illegible]

Accreditation No: 6302
Shop 6A/80 Thorney Rd, Fairfield West
0414 891 998 - Le@LTDesign.net.au

**BUILDING
DESIGNERS
AUSTRALIA**

DRW BY: LT

SCALE: As indicated (A3)

CERTIFICATE NO: 1853942S

"The specifications provided below outline water, thermal performance, material, and energy commitments as per the BASIX certificate. Any discrepancies between the drawings, this summary table, and the original BASIX certificate must be reported immediately to the designer. Always refer to the original BASIX certificate for building construction, materials, insulation requirements, and other details. Please do not solely rely on this summary table, as it only highlights the essential criteria for the purpose of approval."

WATER COMMITMENTS

Showerheads Sytem: Min. 5 star Kitchen Taps: Min. 5 star
Toilet Flushing Sysmtern: Min. 5 star Basin Taps: Min. 5 star
Rainwater Tank: --

THERMAL PERFORMANCE AND MATERIALS COMMITMENTS

EXTERNAL WALLS

Material: External Wall Cladding Insulation: R2.44 (or 3.0 incl. const.)
Wall Colour: Light

INTERNAL WALLS

Materials: Plasterboard on Timber Wall Frame

WINDOWS

Glazing: Clear Glazing Frame : Standard Aluminium Internal cover: Blinds
Eaves: 450mm Window Frame / Glass Specs: Ref. to Basix for details

ROOF

Material: Colorbond Roof Type: Pitch Roof
Roof Colour: Medium (solar absorptance 0.48- 0.59) Insulation: foil/sarking

CEILINGS

Material: Plasterboard Insulation: R3.5 (up)
Ceiling Fan: in living room

FLOORS

Covering: not specified Materials: Concrete Insulation: NIL

ENERGY COMMITMENTS

Hotwater unit : Gas Instantaneous - 5 star
Cooling / Heating System: A/C System 3 star
Ventilation System: Mechanical Vent. System to Kitchen, Bathroom and Laundry
Outdoor Clothes Drying

KITCHEN TAPS - MIN. 5 STAR

BASIN TAPS - MIN. 5 STAR

TOILET FLUSHING SYSTEM - MIN. 5 STAR

SHOWERHEADS - MIN. 5 STAR

MECHANICAL EXHAUST SYSTEM

GAS INSTANTANEOUS WITH A
PERFORMANCE OF 5 STARS

3 STAR A/C UNIT MUST BE 450mm
FROM BOUNDARY AND NOT HIGHER
THAN 1.8m ABOVE GROUND LEVEL

CEILING INSULATION: R3.5 (UP)

EXTERNAL WALL INSULATION: R2.44

EXTERNAL WALL COLOUR: LIGHT

ROOF COLOUR: MEDIUM

450mm ROOF EAVES

1 BASIX COMMITMENTS PLAN
1 : 100

© THIS DRAWING IS THE PROPERTY OF LT DESIGN & CONSULTING PTY LTD AND WE RESERVE THE COPYRIGHT TO ALL OUR DESIGNS WHICH CANNOT BE REPRODUCED (IN PART OR IN WHOLE) BEFORE FIRST OBTAINING WRITTEN CONSENT. CONTRAVENTION WILL BE PROSECUTED

• FIGURED DIMENSIONS TO BE TAKEN IN PREFERENCE TO SCALE.

• BUILDERS' WORK TO COMPLY WITH THE LATEST BCA AND ITS AMENDMENTS AND RELEVANT AUSTRALIAN STANDARDS REFERRED WITHIN.

No.	Description	Date



Building Design | 3D Modeling | Drafting | Detailing



BUILDING
DESIGNERS
AUSTRALIA

Accreditation No: 6302
Shop 6A/80 Thorney Rd, Fairfield West
0414 891 998 - Le@LTDesign.net.au

DRAWING:

BASIX COMMITMENTS PLAN

CLIENT & PROJECT: LOT 288 IN DP 25318

**PROPOSED SECONDARY DWELLING WITH ATTACHED GARAGE
AT: NO.8 IONA STREET, BLACKTOWN, NSW 2148**

COMPLYING DEVELOPMENT CERTIFICATE


DATE:
14/07/2026

DWG NO:
GF-1126-06


SCALE: As indicated (A3)





DRW BY:
LT

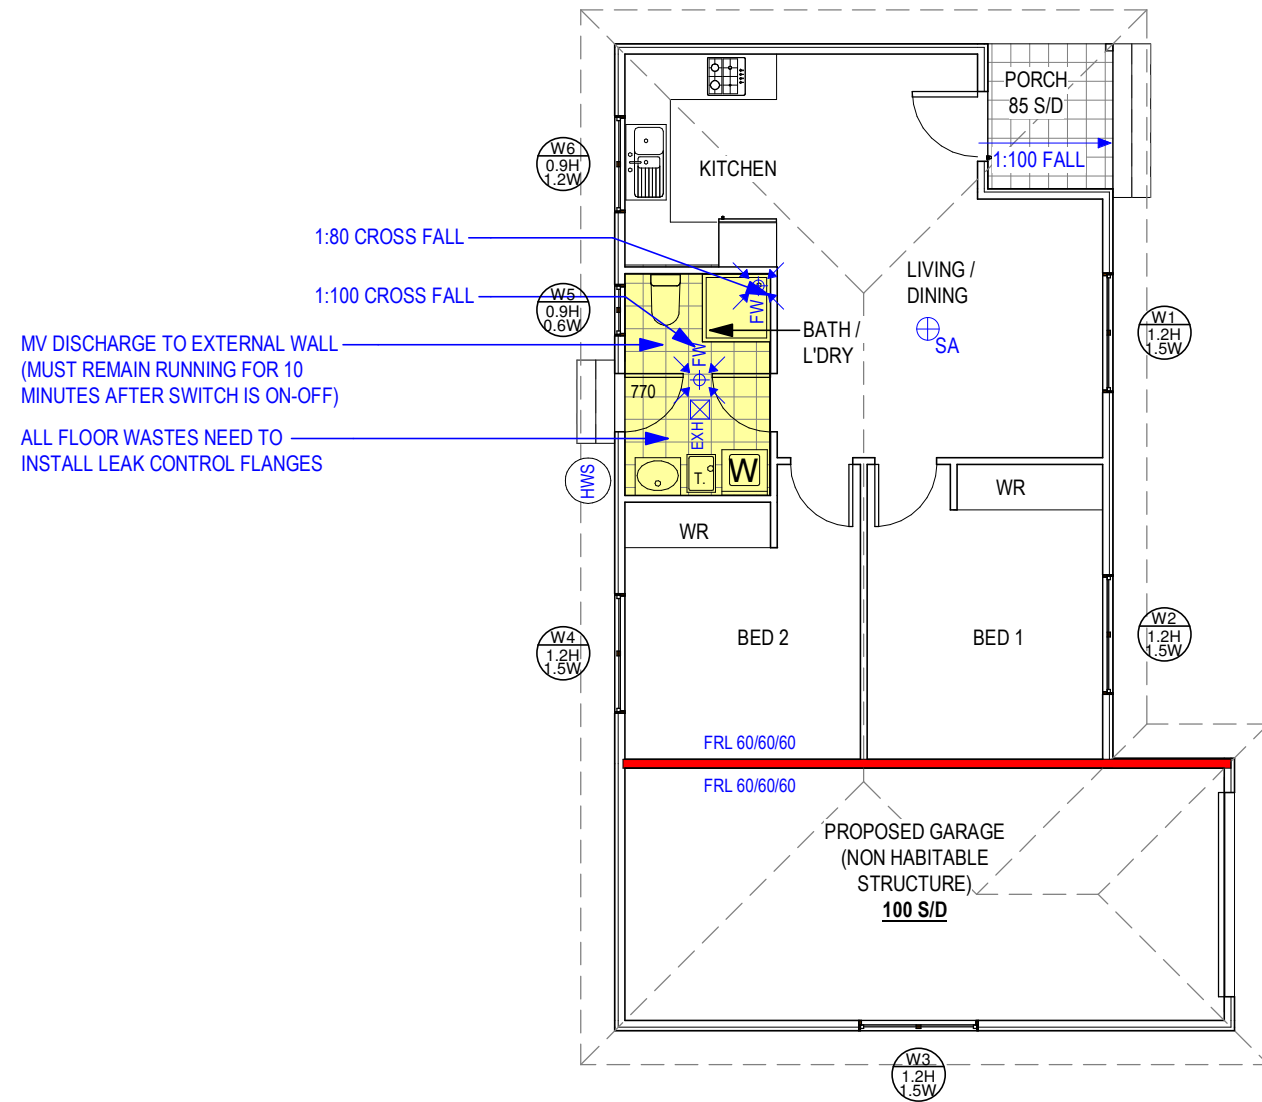

1 WET AREAS PLAN
1 : 100

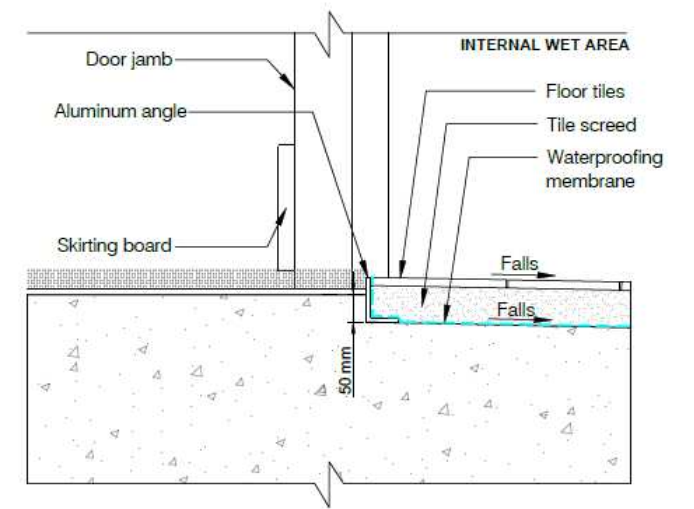

INTERNAL WET AREA DOOR THRESHOLD

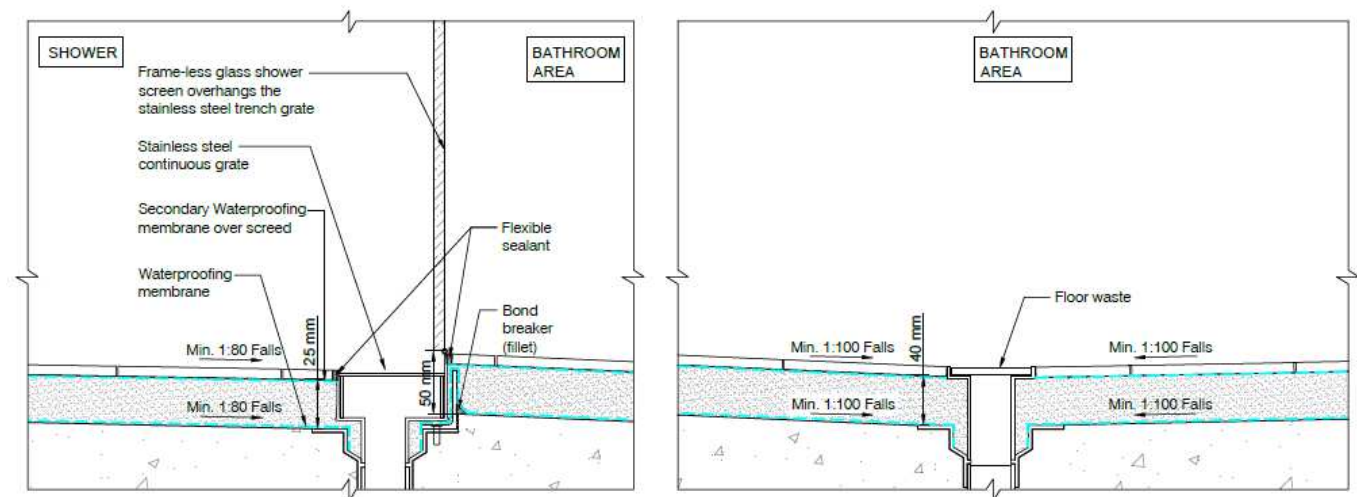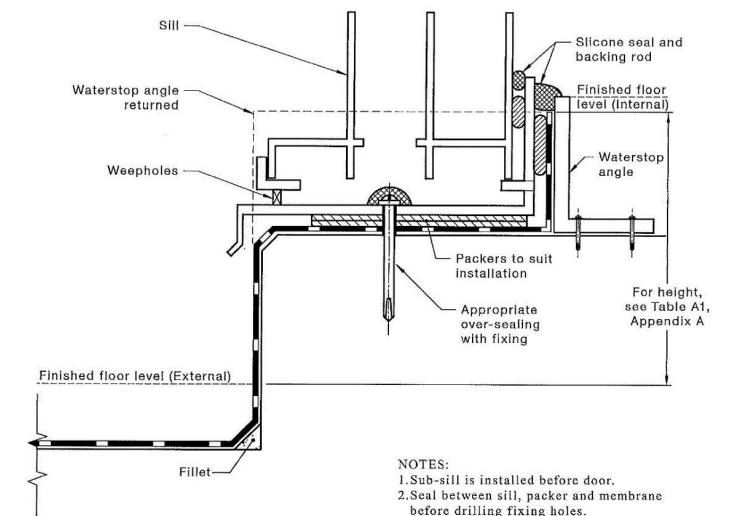

© THIS DRAWING IS THE PROPERTY OF LT DESIGN & CONSULTING PTY LTD AND WE RESERVE THE COPYRIGHT TO ALL OUR DESIGNS WHICH CANNOT BE REPRODUCED (IN PART OR IN WHOLE) BEFORE FIRST OBTAINING WRITTEN CONSENT. CONTRAVENTION WILL BE PROSECUTED

- FIGURED DIMENSIONS TO BE TAKEN IN PREFERENCE TO SCALE.
- BUILDERS' WORK TO COMPLY WITH THE LATEST BCA AND ITS AMENDMENTS AND RELEVANT AUSTRALIAN STANDARDS REFERRED WITHIN.

No.	Description	Date



Building Design | 3D Modeling | Drafting | Detailing



BUILDING DESIGNERS AUSTRALIA
Accreditation No: 6302
Shop 6A/80 Thorney Rd, Fairfield West
0414 891 998 - Le@LTDesign.net.au

DRAWING:
WET AREAS PLAN

CLIENT & PROJECT: LOT 288 IN DP 25318
PROPOSED SECONDARY DWELLING WITH ATTACHED GARAGE
AT: NO.8 IONA STREET, BLACKTOWN, NSW 2148

COMPLYING DEVELOPMENT CERTIFICATE


DATE:
14/07/2026
DWG NO:
GF-1126-07
SCALE:




DRW BY:
LT

1 : 100 (A3)

NOTES:
ALL WATERPROOFING
MUST BE COMPLIED WITH:
- AS 3740:2021
- NCC 2022 - VOLUME 2 -
HOUSING PROVISIONS

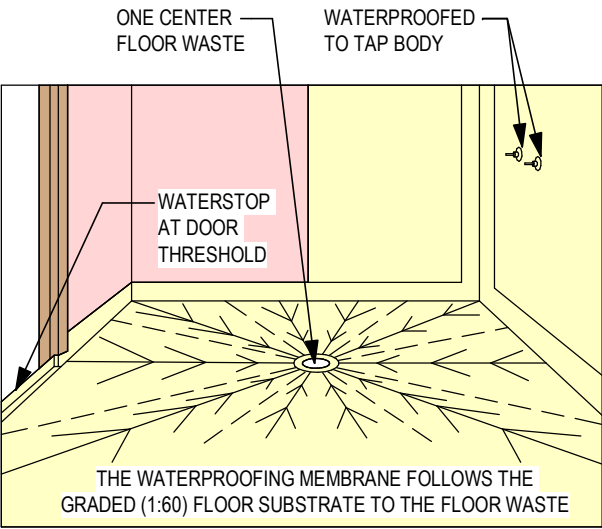

C01 CROSS FALL TO FLOOR WASTE

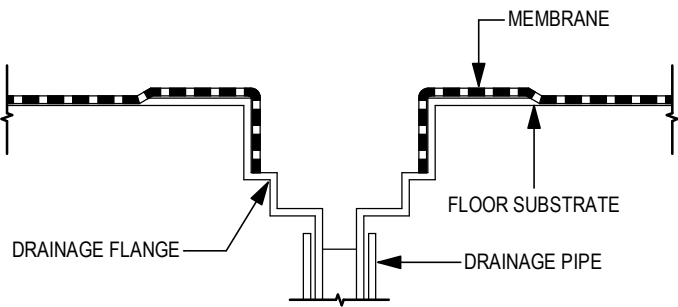


**TYPICAL MEMBRANE TERMINATION
AT DRAINAGE OUTLET**
NOT TO SCALE

C02 LEAK CONTROL FLANGES




**PUDDLE / LEAK CONTROL
DRAINAGE FLANGES**


NOTE: MUST BE APPLIED TO ALL FLOOR WASTES IN WET AREA FOR
GROUND AND UPPER FLOOR / ENTIRE BUILDING
(CLASS 1 BUILDING: CONCRETE FLOOR - MAY SIT ON TOP OF
CONCRETE OR TILE BED FOR - CONCRETE FLOOR ONLY,
OTHER FLOORS - RECESSED INTO FLOOR SUBSTRATE OR TILE BED)

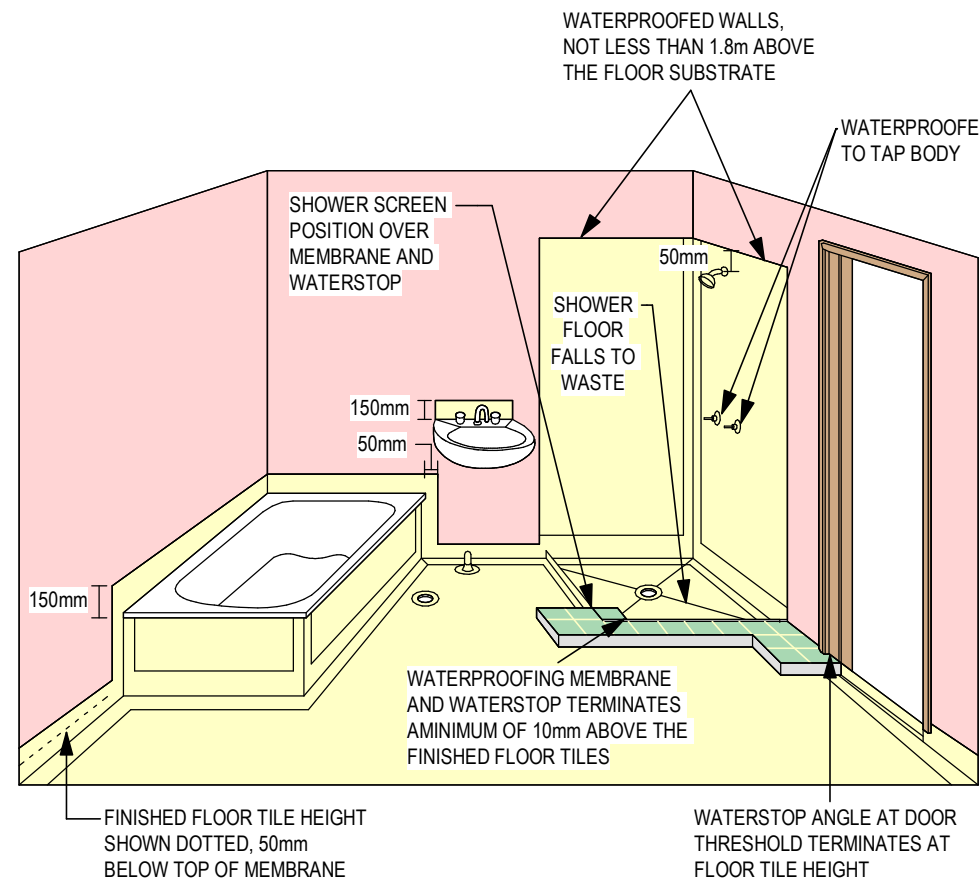

C03 WATERPROOFING DETAILS AROUND BATHROOM

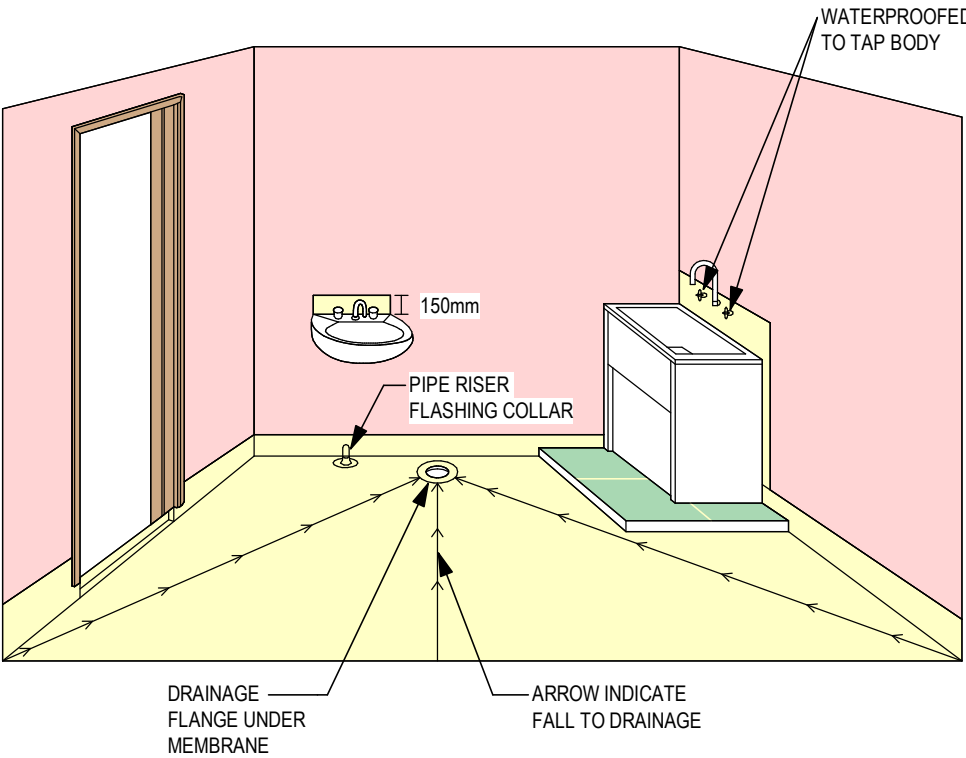

C04 WATERPROOFING DETAILS AROUND LAUNDRY

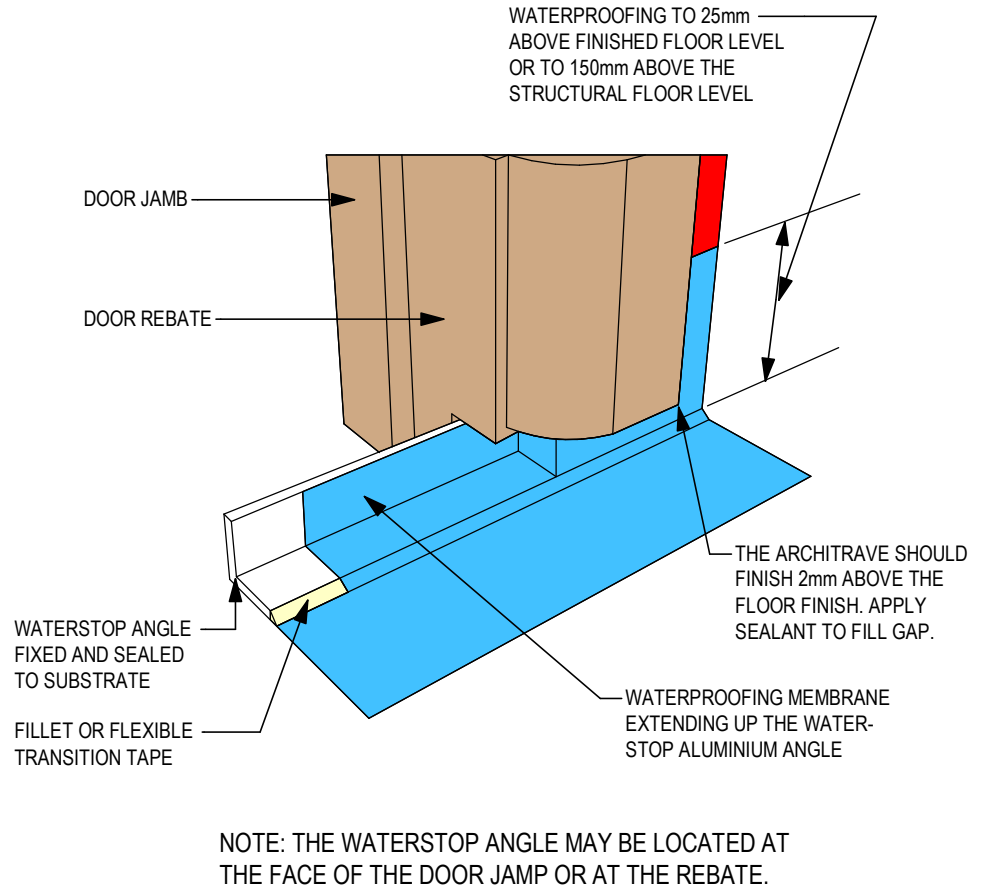

C05 WATERPROOFING UNDER DOOR ARCHITRAVE

© THIS DRAWING IS THE PROPERTY OF LT DESIGN & CONSULTING PTY LTD AND WE RESERVE THE COPYRIGHT TO ALL OUR DESIGNS WHICH CANNOT BE REPRODUCED (IN PART OR IN WHOLE) BEFORE FIRST OBTAINING WRITTEN CONSENT. CONTRAVENTION WILL BE PROSECUTED

- FIGURED DIMENSIONS TO BE TAKEN IN PREFERENCE TO SCALE.
- BUILDERS' WORK TO COMPLY WITH THE LATEST BCA AND ITS AMENDMENTS AND RELEVANT AUSTRALIAN STANDARDS REFERRED WITHIN.

No.	Description	Date



Building Design | 3D Modeling | Drafting | Detailing



BUILDING
DESIGNERS
AUSTRALIA

Accreditation No: 6302
Shop 6A/80 Thorney Rd, Fairfield West
0414 891 998 - Le@LTDesign.net.au

DRAWING:
TYPICAL WATERPROOFING CONSTRUCTION DETAILS

CLIENT & PROJECT: LOT 288 IN DP 25318
**PROPOSED SECONDARY DWELLING WITH ATTACHED GARAGE
AT: NO.8 IONA STREET, BLACKTOWN, NSW 2148**

COMPLYING DEVELOPMENT CERTIFICATE

DATE:
14/07/2026
DWG NO:
GF-1126-08


SCALE:



DRW BY:
LT


1 : 5 (A3)

SYSTEM SPECIFICATIONS Timber Frame Internal Wall Systems – Single Stud

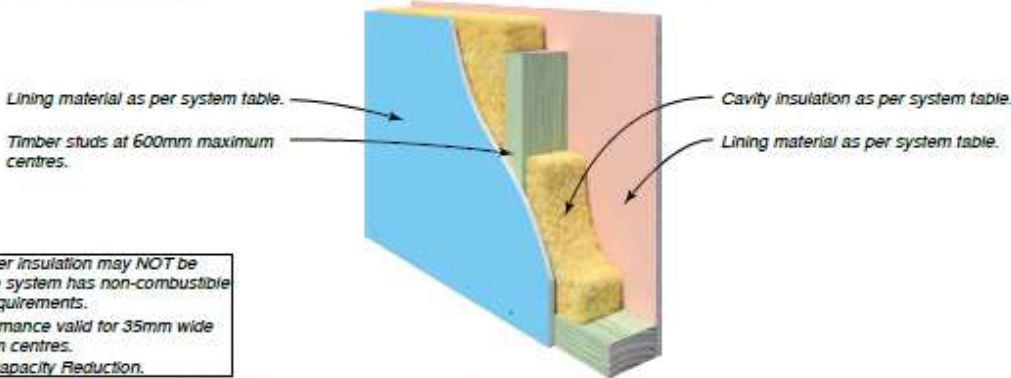


NOTE: Polyester insulation may NOT be used where the system has non-combustible construction requirements.
Acoustic performance valid for 35mm wide studs at 600mm centres.
*ACR = Axial Capacity Reduction.


SYSTEM OPTIONS Refer to Book 2 Residential Installation Guide			ACOUSTIC REPORT: PKA Predictor V16				
FRL Report	SYSTEM N°	WALL LININGS	STUD DEPTH mm	70	90	120	140
			CAVITY INFILL (Refer to TABLE Bii)	R _w / R _w +C _{tr}			
- /60/60 60/60/60 FC 12969		BOTH SIDES • 1 x 16mm Gyprock Fyrchek Plasterboard.	(a) Nil	33/26	36/29	38/32	38/32
			(c) 70 Soundscreen 2.0	39/30	42/33	44/36	43/35
			(e) 75 Gold Batts R2.0	38/29	41/32	42/35	43/35
			(f) 50 MAB Polyester 11kg	36/28	39/31	41/34	40/33
			Wall Thickness mm	102	122	152	172

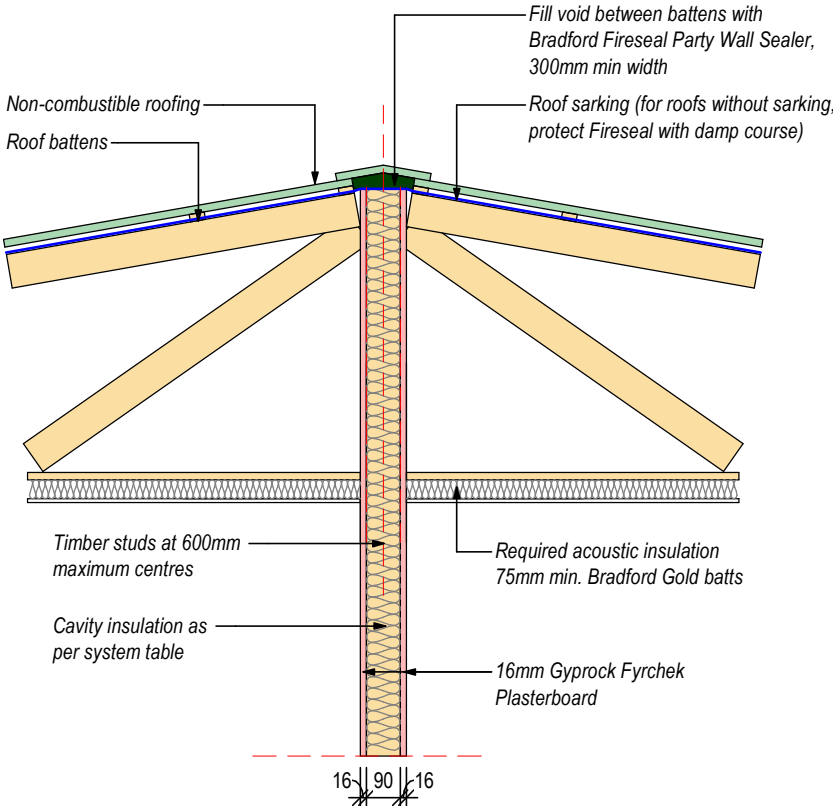

C01 PARTY WALL PERPENDICULAR TO TRUSS/RAFTER (SIDE ELEVATION)

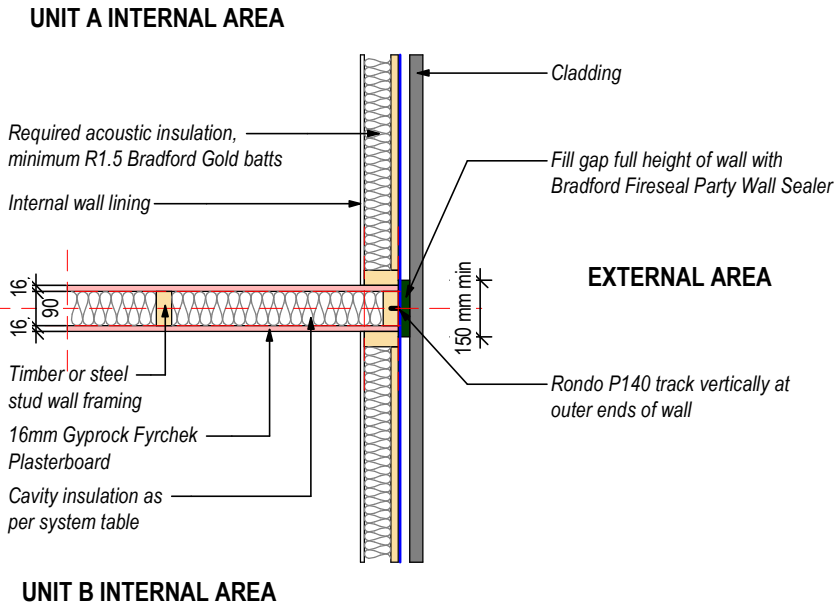

C02 JUNCTION OF PARTY WALL AND EXTERNAL CLADDING - PLAN VIEW

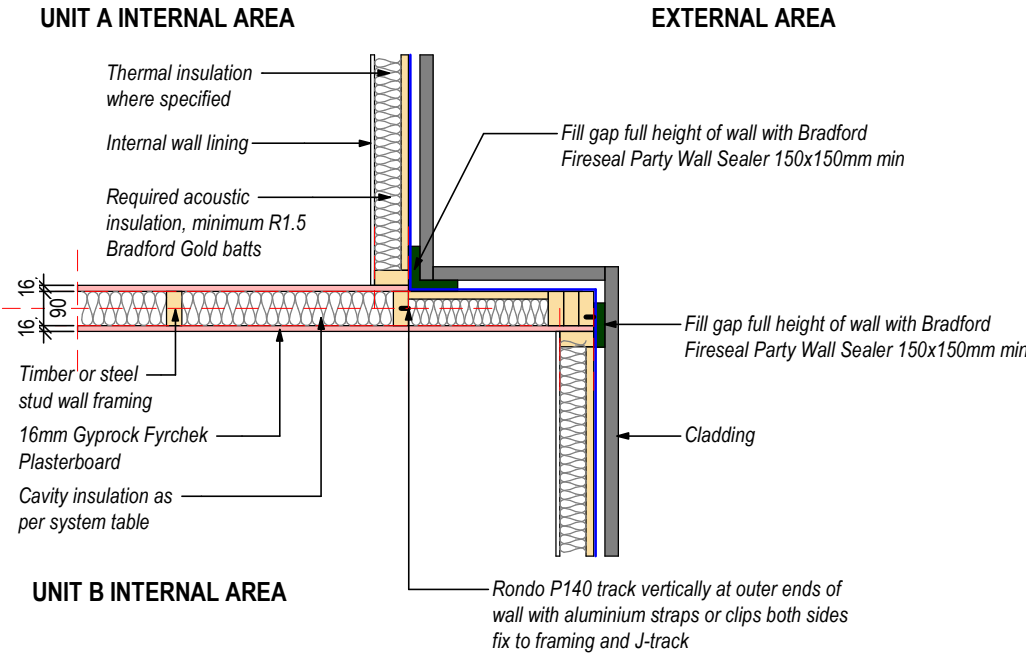

C03 JUNCTION OF PARTY WALL AND EXTERNAL WALL WITH CLADDING AT WALL RETURN - PLAN VIEW

© THIS DRAWING IS THE PROPERTY OF LT DESIGN & CONSULTING PTY LTD AND WE RESERVE THE COPYRIGHT TO ALL OUR DESIGNS WHICH CANNOT BE REPRODUCED (IN PART OR IN WHOLE) BEFORE FIRST OBTAINING WRITTEN CONSENT. CONTRAVENTION WILL BE PROSECUTED

- FIGURED DIMENSIONS TO BE TAKEN IN PREFERENCE TO SCALE.
- BUILDERS' WORK TO COMPLY WITH THE LATEST BCA AND ITS AMENDMENTS AND RELEVANT AUSTRALIAN STANDARDS REFERRED WITHIN.

No.	Description	Date



Building Design | 3D Modeling | Drafting | Detailing



BUILDING DESIGNERS AUSTRALIA
Accreditation No: 6302
Shop 6A/80 Thorney Rd, Fairfield West
0414 891 998 - Le@LTDesign.net.au

DRAWING:
FIREWALL DETAILS - 16MM FYRCHEK SYSTEM

CLIENT & PROJECT: LOT 288 IN DP 25318
PROPOSED SECONDARY DWELLING WITH ATTACHED GARAGE
AT: NO.8 IONA STREET, BLACKTOWN, NSW 2148

COMPLYING DEVELOPMENT CERTIFICATE

DATE:
14/07/2026
DWG NO:
GF-1126-09



DRW BY:
LT

SCALE: 1 : 20 (A3)