

FOR CONSTRUCTION

LOT 11 - 11 SOLSTICE STREET AUSTRAL

PROPOSED CONSTRUCTION OF A TWO STOREY DWELLING



BASIS COMMITMENTS			Certificate number: 18060888
			Date of issue: Friday, 17 July 2020
WATER			
LANDSCAPE	123m2		
TOILETS	4 STARS		
KITCHEN TAPS	4 STARS		
SHOWER HEADS	5 STAR (>4.5 but <=6 Umin)		
BASIN TAPS	4 STARS		
ALTERNATIVE WATER	1500L RAINWATER TANK		
ROOF WATER TO TANK	161m2		
ALT.WATER USES- TANK	LAUNDRY		
ALT. WATER USES - RETIC	ALL TOILETS + ONE OUTDOOR TAP		
SWIMMING POOL	N/A		
ENERGY			
HOT WATER	GAS INSTANTANEOUS - 5 STAR		
AIR-CON (HEATING)	3 PHASE DUCTED - EER 3.0-3.5		
AIR-CON (COOLING)	3 PHASE DUCTED - EER 3.0-3.5		
VENTILATION - BATHROOM	NONE/ NATURAL VENTILATION		
VENTILATION - KITCHEN	DUCTED - MANUAL SWITCH		
VENTILATION - LAUNDRY	NONE/ NATURAL VENTILATION		
PV SYSTEM	N/A		
COOKTOP	GAS		
OVEN	ELECTRIC		
CLOTHES DRYING	OUTDOOR CLOTHESLINE		
LIGHTING	DEDICATED LED		

OnBuild Certifiers Pty Ltd

Reference: 260050

Date: 20/07/2020

GENERAL LEGEND

Andrew Soliman

Director/Principal Certifier

BDC2940

Consultant who prepared this document is responsible for compliance

AC	AIR CONDITIONING UNIT
AD	ALUMINUM DOOR/ WINDOW
BA	BALUSTRADE TYPE
BG	BOX GUTTER
BR1, BR2, etc.	BRICK FACE TYPE
CD1, CD2, etc.	CEMENT CLADDING
CONC.	CONCRETE FLOOR
CPT	CARPET
CRT	CONCRETE ROOF TILES
CR1, CR2, etc.	CEMENT RENDER TYPE/ COLOUR
DPIS	DOWN PIPE
DW	DISH WASHER
ED	ENTRY DOOR
F	FRIDGE
FAS	FASCIA
FET	FEATURE TILE
FT, FT1, FT2, etc.	FLOOR TILES
FW	FLOOR WASTE
GD	GARAGE DOOR
GUT	GUTTER
HWU	HOT WATER UNIT
HYB	HYBRID FLOOR
L	LINEN
MR	METAL ROOF
MW	MICROWAVE OVEN
NGL	NATURAL GROUND LEVEL
OBS	OBSCURED GLASS
P	PANTRY
R	ROBE
RL	REDUCED LEVEL
RWH	RAIN WATER HEAD
RWT	RAIN WATER TANK
S	STORAGE
TOW	TOP OF WALL
TL	TIMBER LAMINATE
WC	WATER CLOSET
WM	WASHING MACHINE
SD	SMOKE DETECTOR

Sheet List				
Sheet No.	Sheet Name	Drawn By	Current Revision Date	Revision
CDC.01	COVER SHEET	AS	02-07-2026	CDC ISSUE
CDC.02A	GENERAL NOTES	AS	30-06-2026	CDC ISSUE
CDC.02B	GENERAL NOTES	AS	30-06-2026	CDC ISSUE
CDC.03	LOCATION PLAN AND SITE PLAN	AS	30-06-2026	CDC ISSUE
CDC.04	SITE ANALYSIS AND SEDIMENT CONTROL	AS	30-06-2026	CDC ISSUE
CDC.05	GROUND FLOOR PLAN	AS	02-07-2026	CDC ISSUE
CDC.06	FIRST FLOOR LEVEL	AS	02-07-2026	CDC ISSUE
CDC.07	ROOF PLAN	AS	02-07-2026	CDC ISSUE

Sheet List				
Sheet No.	Sheet Name	Drawn By	Current Revision Date	Revision
CDC.08	ELEVATION 01	AS	02-07-2026	CDC ISSUE
CDC.09	ELEVATION 02	AS	02-07-2026	CDC ISSUE
CDC.10	SECTIONS	AS	30-06-2026	CDC ISSUE
CDC.11	FLOOR AREA PLAN	AS	02-07-2026	CDC ISSUE
CDC.12	RENTABLE AREA PLAN	AS	30-06-2026	CDC ISSUE
CDC.14	COLOR SCHEDULE	AS	30-06-2026	CDC ISSUE
CDC.15	LANDSCAPE PLAN	AS	30-06-2026	CDC ISSUE
CDC.16	WATERPROOFING DETAILS	AS	30-06-2026	CDC ISSUE

NOTE: ALL IMAGES ARE FOR ILLUSTRATION ONLY AND ARE SUBJECT TO VARIATION AND TO AVAILABILITY OF MATERIALS.

2	02-07-2026	Balcony added and Plan and Facade updated accordingly - Ekta/Biswash		
1	30-06-2026	CDC ISSUE		
REV	DATE	DESCRIPTION	BY	



RUBY HOMES

THIS DRAWING IS THE EXCLUSIVE PROPERTY OF THE DEVELOPER & THE REPRODUCTION OF ANY PART WITHOUT THE PRIOR WRITTEN CONSENT OF THE DEVELOPER IS A VIOLATION OF APPLICABLE LAWS. IN NO EVENT SHALL THE DEVELOPER BE HELD LIABLE FOR SPECIAL, COLLATERAL, INCIDENTAL OR CONSEQUENTIAL LIABILITY IN CONNECTION WITH THE USE OF THIS DIGITAL DATA ONCE RELEASED FROM THE DEVELOPERS OFFICE. THIS DRAWING IS TO BE READ & UNDERSTOOD IN CONJUNCTION WITH THE STRUCTURAL, MECHANICAL, ELECTRICAL &/ OR ANY OTHER CONSULTANT'S DOCUMENTATION AS MAY BE APPLICABLE TO THE PROJECT PRIOR TO THE START OF ANY WORKS AND FOR ITS DURATION.

PROJECT:

Lot 11 11 SOLSTICE STREET

11 SOLSTICE STREET AUSTRAL

DRAWING TITLE:

COVER SHEET

NORTH:

LOT NO:	DATE:	SCALE:	DRAWING No:	REV:
11	20-07-2026	As indicated	CDC.01	2
DRAWN BY:	CHECKED BY:	ISSUED BY:		
AS	RH			
DRAFTED BY:	CLIENT NAME:			
SL	Owner			

BUILDING SPECIFICATIONS

National Construction Code – Volume 2, Amendment 1 – Building Code of Australia 2022 & Housing Provisions Standard 2022

SITE PREPARATION

- PART 3.1 OF THE NCC VOLUME 2, AMENDMENT 1 - BUILDING CODE OF AUSTRALIA 2022 & HOUSING PROVISIONS STANDARD 2022.

EARTHWORKS

- TO BE CARRIED OUT IN ACCORDANCE WITH THE REQUIREMENTS OF THE ENVIRONMENTAL PLANNING & ASSESSMENT ACT 1979 AND DEVELOPMENT CONSENT CONDITIONS
- PART 3.2 OF THE NCC VOLUME 2, AMENDMENT 1 - BUILDING CODE OF AUSTRALIA 2022 & HOUSING PROVISIONS STANDARD 2022.
- AS 4678:2002 - EARTH-RETAINING STRUCTURES

DRAINAGE

- PART 3.3 OF THE NCC VOLUME 2, AMENDMENT 1 - BUILDING CODE OF AUSTRALIA 2022 & HOUSING PROVISIONS STANDARD 2022.
- AS/NZS 3500.1:2021 - PLUMBING & DRAINAGE - WATER SERVICES
- AS/NZS 3500.2:2021 - PLUMBING & DRAINAGE - SANITARY PLUMBING & DRAINAGE
- AS/NZS 3500.3:2021 - PLUMBING & DRAINAGE STORMWATER DRAINAGE
- AS/NZS 3500.4:2021 - PLUMBING & DRAINAGE - HEATED WATER SERVICES

STRUCTURAL WORK

- Part 2.2 OF THE NCC VOLUME 2, AMENDMENT 1 - BUILDING CODE OF AUSTRALIA 2022 & HOUSING PROVISIONS STANDARD 2022.
- AS 4100:2020 - STEEL STRUCTURES CODES
- AS/NZS 1170.0:2002 - GENERAL PRINCIPLES
- AS/NZS 1170.1:2002 - PARTS 1 PERMANENT, IMPOSED AND OTHER ACTIONS
- AS/NZS 1170.2:2021 - PART 2 WIND ACTIONS
- AS 3700:2018 - SAA MASONRY CODE
- AS 1684.3:2021 - RESIDENTIAL TIMBER FRAMED CONSTRUCTION

FOOTINGS & SLABS

- PART 4 OF THE NCC VOLUME 2, AMENDMENT 1 - BUILDING CODE OF AUSTRALIA 2022 & HOUSING PROVISIONS STANDARD 2022.
- AS 2159:2009 - PILING - DESIGN & INSTALLATION
- AS 2870:2011 - RESIDENTIAL SLABS & FOOTINGS
- AS 3600:2018 - CONCRETE STRUCTURES

MASONRY

- PART 5 OF THE NCC VOLUME 2, AMENDMENT 1 - BUILDING CODE OF AUSTRALIA 2022 & HOUSING PROVISIONS STANDARD 2022.
- AS 3700:2018 - MASONRY STRUCTURES

FRAMING

- PART 6 OF THE NCC VOLUME 2, AMENDMENT 1 - BUILDING CODE OF AUSTRALIA 2022 & HOUSING PROVISIONS STANDARD 2022.
- AS 1684.2:2021 - RESIDENTIAL TIMBER-FRAMED CONSTRUCTION - NON- CYCLONIC AREAS
- AS 1720.1:2010 - TIMBER STRUCTURES - DESIGN METHODS
- AS 4100:2020 - STEEL STRUCTURES
- AS 3660.1:2014 - TERMITE MANAGEMENT SYSTEM

ROOF & WALL CLADDING

- PART 7 OF THE NCC VOLUME 2, AMENDMENT 1 - BUILDING CODE OF AUSTRALIA 2022 & HOUSING PROVISIONS STANDARD 2022.
- AS 1273:1991 - UNPLASTICIZED PVC (UPVC) DOWNPIPES & FITTINGS FOR RAINWATER
- AS 1562.1:2018 - DESIGN & INSTALLATION OF SHEET ROOF & WALL CLADDING - METAL
- AS/NZS 1562.3:2006 - DESIGN & INSTALLATION OF SHEET ROOF & WALL CLADDING - PLASTIC
- AS 2049:2002 - ROOF TILES
- AS 2050:2018 - INSTALLATION OF ROOF TILES
- AS 4285:2019 - ROOFLIGHTS

GLAZING

- PART 8 OF THE NCC VOLUME 2, AMENDMENT 1 - BUILDING CODE OF AUSTRALIA 2022 & HOUSING PROVISIONS STANDARD 2022.
- AS 1288:2021 - GLASS IN BUILDINGS - SELECTION & INSTALLATION
- AS 2047:2014 - WINDOWS & EXTERNAL GLAZED DOORS IN BUILDINGS
- AS/NZS 2208:1996 - SAFETY GLAZING MATERIALS IN BUILDINGS

FIRE SAFETY

- PART 9 OF THE NCC VOLUME 2, AMENDMENT 1 - BUILDING CODE OF AUSTRALIA 2022 & HOUSING PROVISIONS STANDARD 2022.
- AS 3786:2014 - SMOKE ALARMS USING SCATTERED LIGHT, TRANSMITTED LIGHT OR IONIZATION

HEALTH & AMENITY

- PART 10 OF THE NCC VOLUME 2, AMENDMENT 1 - BUILDING CODE OF AUSTRALIA 2022 & HOUSING PROVISIONS STANDARD 2022.
- AS/NZS ISO 717.1:2004 - ACOUSTICS - RATING OF SOUND INSULATION IN BUILDINGS & OF BUILDING ELEMENTS - AIRBORNE SOUND INSULATION
- AS ISO 717.2:2004 - ACOUSTICS - RATING OF SOUND INSULATION IN BUILDINGS & OF BUILDING ELEMENTS - IMPACT SOUND INSULATION
- AS 1668.2:2012 - THE USE OF VENTILATION & AIR CONDITIONING IN BUILDINGS - MECHANICAL VENTILATION IN BUILDINGS
- AS 1668.4:2012 - THE USE OF VENTILATION & AIR CONDITIONING IN BUILDINGS - NATURAL VENTILATION OF BUILDINGS
- AS/NZS 1680.0:2009 - INTERIOR LIGHTING - SAFE MOVEMENT
- AS 3740:2021 - WATERPROOFING OF DOMESTIC WET AREAS
- AS 3000:2018 - ELECTRICAL INSTALLATION
- BCA Part 10.8.1, AS4200.1 & AS4200.2 - PLIABLE BUILDING MEMBRANE INSTALLED.

WATERPROOFING

- PART 10.2 OF THE NCC VOLUME 2, AMENDMENT 1 - BUILDING CODE OF AUSTRALIA 2022 & HOUSING PROVISIONS STANDARD 2022
- AS 3740:2021 - WATERPROOFING TO WET AREA
- AS 4654:2012 - EXTERNAL WET AREAS

SAFE MOVEMENT & ACCESS

- PART 11 OF THE NCC VOLUME 2, AMENDMENT 1 - BUILDING CODE OF AUSTRALIA 2022 & HOUSING PROVISIONS STANDARD 2022.
- AS 1428.1:2009 - DESIGN FOR ACCESS & MOBILITY - GENERAL REQUIREMENTS FOR ACCESS - NEW BUILDING WORK
- AS 1657:2018 - FIXED PLATFORMS, WALKWAYS, STAIRWAYS & LADDERS - DESIGN, CONSTRUCTION & INSTALLATION

HANDRAILS & BALUSTRADES

- PART 11.3.3 OF THE NCC VOLUME 2, AMENDMENT 1 - BUILDING CODE OF AUSTRALIA 2022 & HOUSING PROVISIONS STANDARD 2022.
- PART 11.3.4 OF THE NCC VOLUME 2, AMENDMENT 1 - BUILDING CODE OF AUSTRALIA 2022 & HOUSING PROVISIONS STANDARD 2022.
- PART 11.3.5 OF THE NCC VOLUME 2, AMENDMENT 1 - BUILDING CODE OF AUSTRALIA 2022 & HOUSING PROVISIONS STANDARD 2022.
- AS 1170.1:2002 - BALUSTRADE INSTALLATION

PROTECTION OF OPENABLE WINDOW


PART 11.3.7 AND 11.3.8 OF THE NCC VOLUME 2, AMENDMENT 1 - BUILDING CODE OF AUSTRALIA 2022 & HOUSING PROVISIONS STANDARD 2022.

ENERGY EFFICIENCY

- PART 13 OF THE NCC VOLUME 2, AMENDMENT 1 - BUILDING CODE OF AUSTRALIA 2022 & HOUSING PROVISIONS STANDARD 2022 & BASIX CERTIFICATE.

MECHANICAL VENTILATION

- EXHAUST FROM A BATHROOM, SANITARY COMPARTMENT TO DISCHARGE DIRECTLY TO OUTDOOR AIR WITH MINIMUM FLOW RATE OF 25L/S & MAKE-UP AIR VIA OPENINGS TO AN ADJACENT ROOM WITH A FREE AREA OF 14,000 MM². THIS EXHAUST SYSTEM MUST BE INTERLOCKED WITH LIGHT SWITCH AND INCLUDE RUN-ON TIMER SO THAT THE EXHAUST SYSTEM CONTINUES TO OPERATE FOR 10 MINUTES AFTER THE LIGHT SWITCH IS OFF.
- ANY INSTALLED - KITCHEN RANGEHOOD EXHAUST TO DISCHARGE DIRECTLY OR VIA DUCT TO OUTDOOR AIR WITH MINIMUM FLOW RATE OF 40L/S & MAKE-UP AIR VIA OPENINGS TO AN ADJACENT ROOM WITH A FREE AREA OF 14,000 MM².
- LAUNDRY EXHAUST TO DISCHARGE DIRECTLY OR VIA DUCT TO OUTDOOR AIR WITH MINIMUM FLOW RATE OF 40L/S & MAKE-UP AIR VIA OPENINGS TO AN ADJACENT ROOM WITH A FREE AREA OF 14,000 MM².

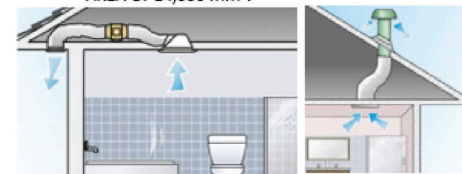

REV	DATE	DESCRIPTION	BY
1	30-06-2026	CDC ISSUE	



THIS DRAWING IS THE EXCLUSIVE PROPERTY OF THE DEVELOPER & THE REPRODUCTION OF ANY PART WITHOUT THE PRIOR WRITTEN CONSENT OF THE DEVELOPER IS A VIOLATION OF APPLICABLE LAWS. IN NO EVENT SHALL THE DEVELOPER BE HELD LIABLE FOR SPECIAL, COLLATERAL, INCIDENTAL OR CONSEQUENTIAL LIABILITY IN CONNECTION WITH THE USE OF THIS DIGITAL DATA ONCE RELEASED FROM THE DEVELOPER'S OFFICE. THIS DRAWING IS TO BE READ & UNDERSTOOD IN CONJUNCTION WITH THE STRUCTURAL, MECHANICAL, ELECTRICAL & / OR ANY OTHER CONSULTANT'S DOCUMENTATION AS MAY BE APPLICABLE TO THE PROJECT PRIOR TO THE START OF ANY WORKS AND FOR ITS DURATION.

PROJECT:

Lot 11 11 SOLSTICE STREET
11 SOLSTICE STREET
AUSTRAL

DRAWING TITLE:

GENERAL NOTES

NORTH:

LOT NO:	DATE:	SCALE:	DRAWING No:	REV:
11	20-07-2026	1 : 2	CDC.02A	1
DRAWN BY:	CHECKED BY:	CLIENT NAME:	ISSUED BY:	
AS	RH	Owner		
DRAFTED BY:				
SL				

CDC ISSUE

CDC.02A

TERMITE SHEET

- TERMITE SHEET EXTENDS THROUGH THE ENTIRE MASONRY LEAF AND IS VISIBLE AT THE FINISHED FACE OF THE WALL.


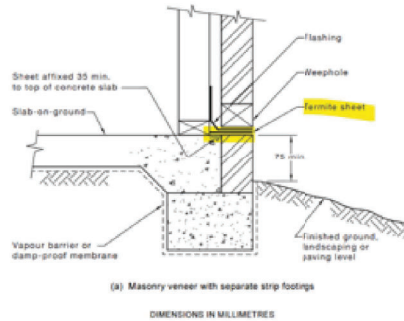


FIGURE 5.5 (in part) TYPICAL SHEET INSTALLATION TO EXTERNAL WALL WITH CONCRETE FLOOR SLAB

DPC FOR BRICKS

DAMP-PROOF COURSE (DPC) TO EXTENDS THROUGH THE ENTIRE MASONRY LEAF AND NEED TO BE VISIBLE AT THE FINISHED FACE OF THE WALL FROM OUTSIDE

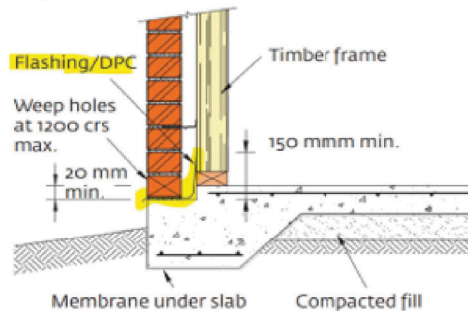

DEMOLITION

- AS 2601-2001 – DEMOLITION WORK

PLANTER BOX

REFER BELOW DETAILS FOR PLANTER BOX.



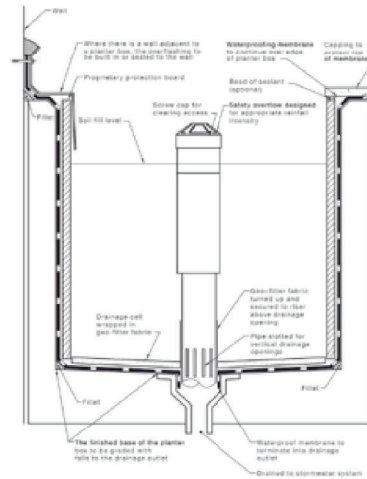


FIGURE 2.17 TYPICAL PLANTER BOX CONSTRUCTION

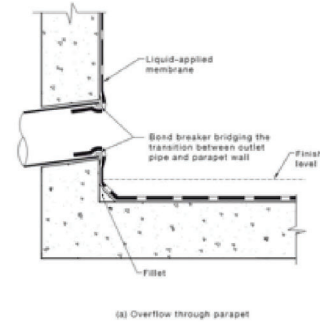

OVERFLOW TO BALCONY:

- SURFACE DRAIN & OVERFLOW TO BALCONY

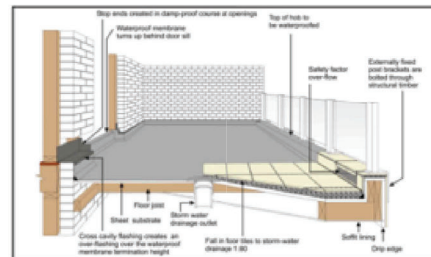

SWIMMING POOL

- PART 12.1.1 (H7D2) OF THE NCC VOLUME 2, AMENDMENT 1 - BUILDING CODE OF AUSTRALIA 2022 & HOUSING PROVISIONS STANDARD 2022
- AS 1926 PART 1-2012 – SWIMMING POOLSAFETY- SAFETY BARRIERS FOR SWIMMING POOLS
- AS 1926 PART 2-2007 - SWIMMING POOL SAFETY- LOCATION OF SAFETY BARRIERS FOR SWIMMING POOLS (INCORPORATING AMENDMENTS 1 AND 2)
- AS 1926 PART 3-2010 – SWIMMING POOL SAFETY- WATER RECIRCULATION SYSTEMS (INCORPORATING AMENDMENT 1)

OnBuild Certifiers Pty Ltd

Reference: 260050

Date: 27/07/2026

Andrew Soliman

Director/ Principal Certifier

BDC2940

Consultant who prepared this document remains responsible for accuracy

REV	DATE	DESCRIPTION	BY
1	30-06-2026	CDC ISSUE	



RUBY HOMES

THIS DRAWING IS THE EXCLUSIVE PROPERTY OF THE DEVELOPER & THE REPRODUCTION OF ANY PART WITHOUT THE PRIOR WRITTEN CONSENT OF THE DEVELOPER IS A VIOLATION OF APPLICABLE LAWS. IN NO EVENT SHALL THE DEVELOPER BE HELD LIABLE FOR SPECIAL COLLATERAL, INCIDENTAL OR CONSEQUENTIAL LIABILITY IN CONNECTION WITH THE USE OF THIS DIGITAL DATA ONCE RELEASED FROM THE DEVELOPERS OFFICE. THIS DRAWING IS TO BE READ & UNDERSTOOD IN CONJUNCTION WITH THE STRUCTURAL, MECHANICAL, ELECTRICAL & / OR ANY OTHER CONSULTANT'S DOCUMENTATION AS MAY BE APPLICABLE TO THE PROJECT PRIOR TO THE START OF ANY WORKS AND FOR ITS DURATION.

PROJECT:
Lot 11 11 SOLSTICE STREET
11 SOLSTICE STREET AUSTRAL

DRAWING TITLE:
GENERAL NOTES

NORTH:

LOT NO:

11

DRAWN BY:

AS

DRAFTED BY:

SL

DATE:

20-07-2026

SCALE:

1 : 2

CDC ISSUE


DRAWING No: REV: 1

CDC.02B

ISSUED BY:


CLIENT NAME:

Owner

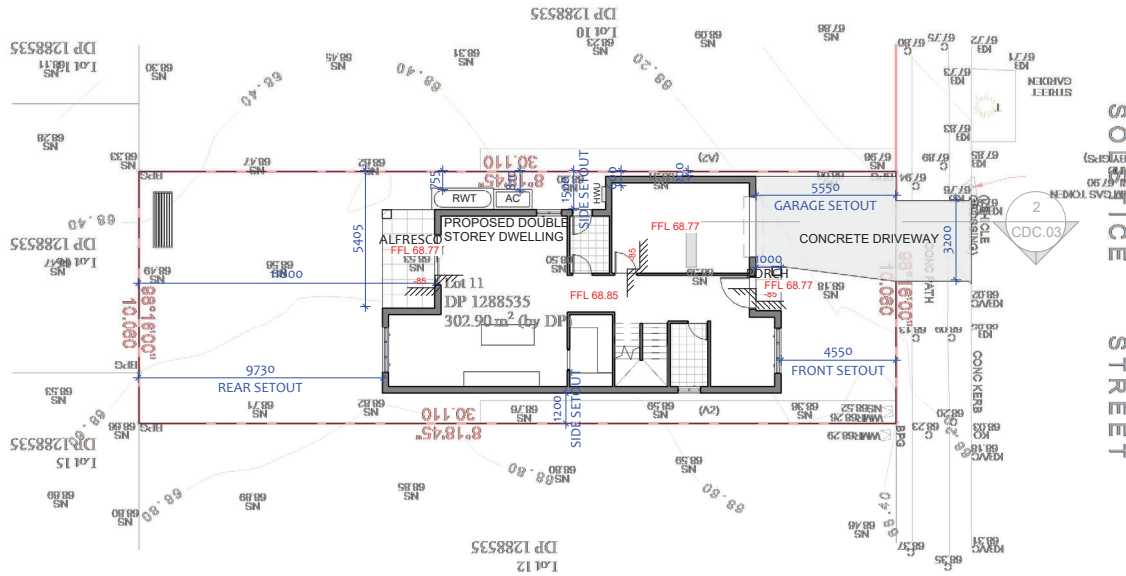

CDC - SITE PLAN

1 : 200

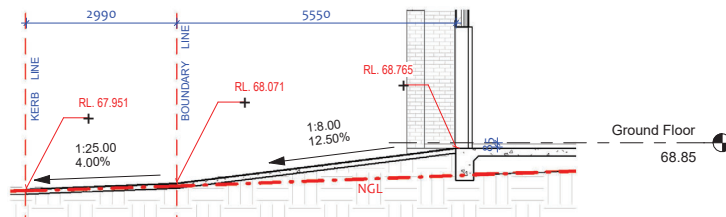

DRIVEWAY SECTION

1 : 100

OnBuild Certifiers Pty Ltd
Reference: 260050
Date: 27/07/2026

AREA SCHEDULE	
Director/ Principal Certifier	AREA (m2)
BDC2940	
LOT AREA	302.9
GROUND FLOOR	81
FIRST FLOOR	79
GARAGE	20
STAIRCASE VOID	5
PRIVATE OPEN SPACE	24
DRIVEWAY	23
FRONT LANDSCAPE	25.9
REAR LANDSCAPE	97.8

GREENFIELD HOUSING CODE COMPLIANCE TABLE

DESCRIPTION		COMPLIANCE		COMMENT
ELEMENT	CODE CONTROL	REQUIREMNT	PROPOSED	
LOAND ZONE	R2: LOW DENSITY RESIDENTIAL			
LOT NO	LOT 11			
LOT AREA	302.9 m2			
LOT WIDTH	Standard Lot Min. 6m at Building Line facing primary road	6.0m	10.06 m	YES
HEIGHT	MAX. Height	8.5m	8m (MAX.)	YES
FRONT SETBACK	FRONT SET BACK (Min. Setback from Primary Road) For 300-350 sqm. Lot	4.5 m	4.55m	YES
REAR SET BACK (MIN.)	GROUND FLOOR	3m	9.6 m	YES
	FIRST FLOOR	6m	11.8 m	
SIDE SET BACK (MIN.)	GROUND FLOOR	0/0.9m	0.2/1.2m	YES
	FIRST FLOOR	1.2/0.9m	1.5/1.2m	
GROSS FLOOR AREA (GFA)	235 sqm.	235.00m2	162 m2	YES
GROSS FLOOR AREA PLAN	GROUND FLOOR		81 m2	
	FIRST FLOOR		79 m2	
ROOF AREA			162 m2	
GARAGE			20 m2	
PRIVATE OPEN SPACE	>10m Lot width	24m2	24 m2	YES
LANDSCAPE AREA	15 % of TOTAL LAND AREA	45.435 m2	123.7 m2	YES

CDC ISSUE

REV	DATE	DESCRIPTION	BY
1	30-06-2026	CDC ISSUE	




THIS DRAWING IS THE EXCLUSIVE PROPERTY OF THE DEVELOPER & THE REPRODUCTION OF ANY PART WITHOUT THE PRIOR WRITTEN CONSENT OF THE DEVELOPER IS A VIOLATION OF APPLICABLE LAWS. IN NO EVENT SHALL THE DEVELOPER BE HELD LIABLE FOR SPECIAL, COLLATERAL, INCIDENTAL OR CONSEQUENTIAL LIABILITY IN CONNECTION WITH THE USE OF THIS DIGITAL DATA ONCE RELEASED FROM THE DEVELOPER'S OFFICE. THIS DRAWING IS TO BE READ & UNDERSTOOD IN CONJUNCTION WITH THE STRUCTURAL, MECHANICAL, ELECTRICAL &/OR ANY OTHER CONSULTANT'S DOCUMENTATION AS MAY BE APPLICABLE TO THE PROJECT PRIOR TO THE START OF ANY WORKS AND FOR ITS DURATION.

PROJECT:
Lot 11 11 SOLSTICE STREET
11 SOLSTICE STREET AUSTRAL

DRAWING TITLE:
LOCATION PLAN AND SITE PLAN



LOT NO:	11	DATE:	20-07-2026	SCALE:	As indicated	DRAWING No:	CDC.03	REV:	1
DRAWN BY:	AS	CHECKED BY:	RH					ISSUED BY:	
DRAFTED BY:	SL	CLIENT NAME:	Owner						




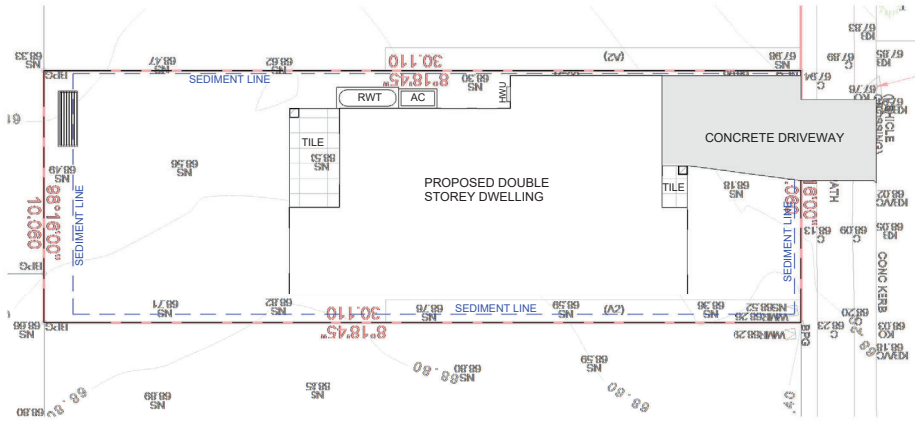


CDC - SITE ANALYSIS AND SEDIMENT CONTROL PLAN

1 : 200

SD 5-7 STABILISED SITE ACCESS

- 1) STRIP TOPSOIL AND LEVEL SITE.
- 2) COMPACT SUBGRADE.
- 3) COVER AREA WITH GEOTEXTILE.
- 4) CONSTRUCT 200 mm THICK PAD OVER GEOTEXTILE USING ROADBASE OR 30 mm AGGREGATE. Min 15 m LONG OR TO BUILDING ALIGNMENT. Min 3 m WIDE.
- 5) CONSTRUCT HUMP IMMEDIATELY WITHIN BOUNDARY TO DIVERT WATER TO A SEDIMENT FENCE OR OTHER SEDIMENT TRAP.

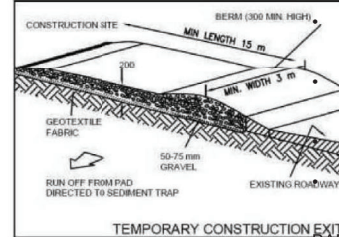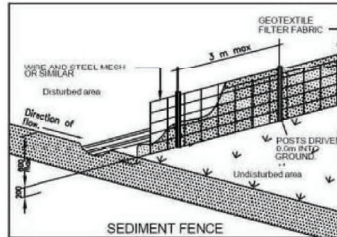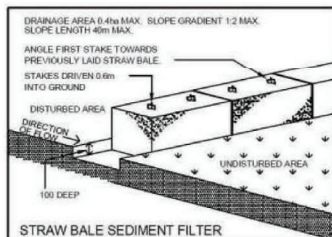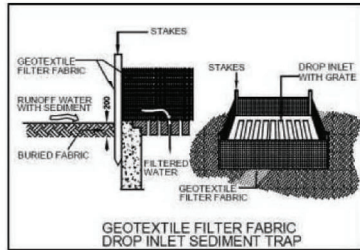

TEMPORARY 1.8M HIGH WIRE MESH FENCE WITH DUSTPROOF MESH APPLIED TO FULL HEIGHT TO BOUNDARIES AS REQUIRED

LOCATION OF WASTE BINS
SEDIMENT FENCE AS REQUIRED
GRAVEL ACCESS
SITE ACCESS AREA TO BE USED FOR WASHDOWN AREA
FOOTPATH CLEAN AND CLEAR AT ALL TIMES
LOCATION OF STOCKPILE MATERIAL
MATERIAL STORAGE AREA
TEMPORARY TOILETS
INSTALL TEMPORARY SEDIMENT BARRIERS TO ALL INLET PITS LIKELY TO COLLECT SILT LADEN WATER, TO COUNCIL'S REQUIREMENTS.

SD 6-9 GEOTEXTILE INLET FILTER

- 1) FABRICATE A SEDIMENT BARRIER MADE FROM GEOTEXTILE. REFER SD6-7 FOR DETAILS.
- 2) SUPPORT GEOTEXTILE WITH MESH TIED TO POSTS AT 1 m Ctrs.
- 3) DO NOT COVER INLET WITH GEOTEXTILE.

SITE WORKS NOTES

1. ORIGIN OF LEVELS PROVIDED BY SURVEYOR
2. THE BUILDER SHALL VERIFY ALL DIMENSIONS AND EXISTING LEVELS ON SITE PRIOR TO THE COMMENCEMENT OF WORK AND ANY DISCREPANCIES SHALL BE REPORTED TO THE SURVEYOR / ENGINEER.
3. TOPSOIL SHALL BE STRIPPED FROM THE CONSTRUCTION AREA AND STOCKPILED ON SITE, TO BE LATER SPREAD OR DISPOSED OFF SITE, AS DIRECTED BY SUPERVISOR / ENGINEER.
4. ALL TRENCH BACKFILL MATERIAL SHALL BE COMPACTED TO THE SAME DENSITY AS THE ADJACENT MATERIAL.
5. ALL SERVICE TRENCHES UNDER VEHICULAR PAVEMENTS SHALL BE BACKFILLED WITH SAND OR APPROVED GRANULAR MATERIALS, TO THE UNDERSIDE OF THE PAVEMENT, AND COMPACTED TO 98% STANDARD MAXIMUM DRY DENSITY, IN ACCORDANCE WITH AS 1289E1.1.

SEDIMENT AND EROSION NOTES

- THIS PLAN IS TO BE READ IN CONJUNCTION WITH SEDIMENT AND EROSION CONTROL DETAILS AS ATTACHED.
- THE CONTRACTOR SHALL IMPLEMENT ALL SOIL EROSION AND SEDIMENT CONTROL MEASURES AS NECESSARY AND TO THE SATISFACTION OF COUNCIL PRIOR TO THE COMMENCEMENT AND DURING CONSTRUCTION. NO DISTURBANCE TO THE SITE SHALL BE PERMITTED OTHER THAN IN THE IMMEDIATE AREA OF THE WORK AND NO MATERIAL SHALL BE REMOVED FROM THE SITE WITHOUT COUNCIL'S APPROVAL. ALL SEDIMENT AND EROSION CONTROL DEVICES TO BE INSTALLED AND MAINTAINED IN ACCORDANCE WITH STANDARDS OUTLINED IN NSW DEPARTMENT OF HOUSING "MANAGING URBAN STORMWATER-SOILS AND CONSTRUCTIONS".
- TOPSOIL SHALL BE STRIPPED AND STOCKPILED OUTSIDE HAZARD AREAS SUCH AS DRAINAGE LINES. THIS TOP SOIL IS TO BE RESPIRED LATER ON AREAS TO BE REVEGETATED AND STABILISED ONLY. (I.E ALL FOOTPATHS, BATTERS, SITE REGARDING AREAS, BASINS AND CATCH DRAINS). TOPSOIL SHALL NOT BE RESPIRED ON ANY OTHER AREAS UNLESS SPECIALLY INSTRUCTED BY THE SUPERINTENDENT. IF THEY ARE TO REMAIN FOR LONGER THAN ONE MONTH STOCKPILES SHALL BE PROTECTED FROM EROSION BY COVERING THEM WITH A MULCH AND HYDROSEEDING AND, IF NECESSARY, BY LOCATING BANKS OR DRAINS DOWNSTREAM OF A STOCKPILE TO RETARD SILT LADEN RUNOFF.
- THE CONTRACTOR SHALL REGULARLY MAINTAIN ALL SEDIMENT AND EROSION CONTROL DEVICES AND REMOVE ACCUMULATED SILT FROM SUCH DEVICES SUCH THAT MORE THAN 60% OF THEIR CAPACITY LOST. ALL THE SILTS TO BE PLACED OUTSIDE THE LIMIT OF WORKS. THE PERIOD FOR MAINTAINING THESE DEVICES SHALL BE AT LEAST UNTIL ALL DISTURBED AREAS ARE REVEGETATED AND FURTHER AS MAY BE DIRECTED BY THE SUPERINTENDENT OR COUNCIL.
- LAY TURF STRIP (MIN 300 mm WIDE) ON 100 mm TOPSOIL WITH 1.0 m LONG RETURNS EVERY 6.0m BEHIND ALL KERB AT THE TOP OF ALL BATTERS AND AROUND STRUCTURES IMMEDIATELY AFTER BACKFILLING OR FORMATION.
- THE CONTRACTOR SHALL GRASS SEED ALL DISTURBED AREAS WITH AN APPROVED MIX AS SSON AS PRACTICABLE AFTER COMPLETION OF EARTHWORKS AND REGRADING.
- VEHICULAR TRAFFIC SHALL BE CONTROLLED DURING CONSTRUCTION CONFINING ACCESS WHERE POSSIBLE TO NOMINATED STABILISED ACCESS POINTS.
- WHEN ANY DEVICES ARE TO BE HANDED OVER TO COUNCIL, THEY SHALL BE IN CLEAN AND STABLE CONDITION.
- THE CONTRACTOR SHALL IMPLEMENT DUST CONTROL BY REGULAR WETTING DOWN (BUT NOT SATURATING) DISTURBED AREA.
- PROVIDE AND MAINTAIN SILT TRAPS AROUND ALL SURFACE INLET PITS UNTIL CATCHMENT IS REVEGETATED OR PAVED.
- REVEGETATE ALL TRENCHES IMMEDIATELY UPON COMPLETION OF BACKFILLING.
- ALL DRAINAGE PIPE INLETS TO BE CAPPED UNTIL:
A) DOWNPIPES CONNECTED
B) PITS CONSTRUCTED & PROTECTED WITH SILT BARRIER

REV	DATE	DESCRIPTION	BY
1	30-06-2026	CDC ISSUE	


RUBY HOMES
THIS DRAWING IS THE EXCLUSIVE PROPERTY OF THE DEVELOPER & THE REPRODUCTION OF ANY PART WITHOUT THE PRIOR WRITTEN CONSENT OF THE DEVELOPER IS A VIOLATION OF APPLICABLE LAWS. IN NO EVENT SHALL THE DEVELOPER BE HELD LIABLE FOR SPECIAL, COLLATERAL, INCIDENTAL OR CONSEQUENTIAL LIABILITY IN CONNECTION WITH THE USE OF THIS DIGITAL DATA ONCE RELEASED FROM THE DEVELOPER'S OFFICE. THIS DRAWING IS TO BE READ & UNDERSTOOD IN CONJUNCTION WITH THE STRUCTURAL, MECHANICAL, ELECTRICAL & / OR ANY OTHER CONSULTANT'S DOCUMENTATION AS MAY BE APPLICABLE TO THE PROJECT PRIOR TO THE START OF ANY WORKS AND FOR ITS DURATION.

PROJECT:
Lot 11 11 SOLSTICE STREET
11 SOLSTICE STREET
AUSTRAL

DRAWING TITLE:
SITE ANALYSIS
AND SEDIMENT
CONTROL



LOT NO:	DATE:	SCALE:	DRAWING No:	REV:
11	20-07-2026	As indicated	CDC.04	1
DRAWN BY:	CHECKED BY:	CLIENT NAME:	ISSUED BY:	
AS	RH	Owner		
DRAFTED BY:				
SL				

OnBuild Construction Ltd
 Reference: 11111111
 Date: 20-07-2026
 Andrew Solomon
 Director/ Principal Designer
 BPC 35441
 Consultant who prepared this document remains responsible for accuracy

IMPORTANT NOTES:
 ALL DIMENSIONS AND NOTES ON ALL PLANS MUST BE CHECKED AND VERIFIED BY BUILDERS AND OWNER PRIOR TO COMMENCEMENT OF ANY BUILDING WORKS. TO CLARIFY AND CONFIRM WITH CONSTRUCTION COMPANY FOR DISCREPANCIES ON ALL DOCUMENTS AND PLANS PROVIDED FOR CONSTRUCTION. ANY WORK INDICATED ON THE PLAN BUT NOT IN CONTRACT, VARIATION TO PLANS. SPECIFICATIONS MAY NOT BE THE RESPONSIBILITY OF THE BUILDER. END USER TO VERIFY PLANS CURRENT BCA AND AUSTRALIAN STANDARDS. WINDOWS TO COMPLY WITH 3.9.3.5 OF THE BCA.



NOTE: PLEASE REFER TO TENDER FOR ALL INCLUSIONS.

REV	DATE	DESCRIPTION	BY
2	02-07-2026	Balcony added and Plan and Facade updated accordingly - Ekta/Biswash	
1	30-06-2026	CDC ISSUE	


RUBY HOMES

THIS DRAWING IS THE EXCLUSIVE PROPERTY OF THE DEVELOPER & THE REPRODUCTION OF ANY PART WITHOUT THE PRIOR WRITTEN CONSENT OF THE DEVELOPER IS A VIOLATION OF APPLICABLE LAWS. IN NO EVENT SHALL THE DEVELOPER BE HELD LIABLE FOR SPECIAL COLLATERAL, INCIDENTAL OR CONSEQUENTIAL LIABILITY IN CONNECTION WITH THE USE OF THIS DIGITAL DATA ONCE RELEASED FROM THE DEVELOPER'S OFFICE. THIS DRAWING IS TO BE READ & UNDERSTOOD IN CONJUNCTION WITH THE STRUCTURAL, MECHANICAL, ELECTRICAL &/OR ANY OTHER CONSULTANT'S DOCUMENTATION AS MAY BE APPLICABLE TO THE PROJECT PRIOR TO THE START OF ANY WORKS AND FOR ITS DURATION.

PROJECT: Lot 11 11 SOLSTICE STREET 11 SOLSTICE STREET AUSTRAL	DRAWING TITLE: GROUND FLOOR PLAN	NORTH: 	LOT NO: 11	DATE: 20-07-2026	SCALE: 1 : 100	DRAWING No: CDC.05	REV: 2
			DRAWN BY: AS	CHECKED BY: RH			ISSUED BY:
			DRAFTED BY: SL	CLIENT NAME: Owner			

OnBuild Construction Ltd
Reference: 2026/07/07
Date: 20-07-2026
Andrew Solomon
Director/ Principal Designer
BPC TEAM
Consultant who prepared this document remains responsible for accuracy

IMPORTANT NOTES:
ALL DIMENSIONS AND NOTES ON ALL PLANS MUST BE CHECKED AND VERIFIED BY BUILDERS AND OWNER PRIOR TO COMMENCEMENT OF ANY BUILDING WORKS. TO CLARIFY AND CONFIRM WITH CONSTRUCTION COMPANY FOR DISCREPANCIES ON ALL DOCUMENTS AND PLANS PROVIDED FOR CONSTRUCTION. ANY WORK INDICATED ON THE PLAN BUT NOT IN CONTRACT, VARIATION TO PLANS. SPECIFICATIONS MAY NOT BE THE RESPONSIBILITY OF THE BUILDER. END USER TO VERIFY PLANS CURRENT BCA AND AUSTRALIAN STANDARDS. WINDOWS TO COMPLY WITH 3.9.3.5 OF THE BCA.

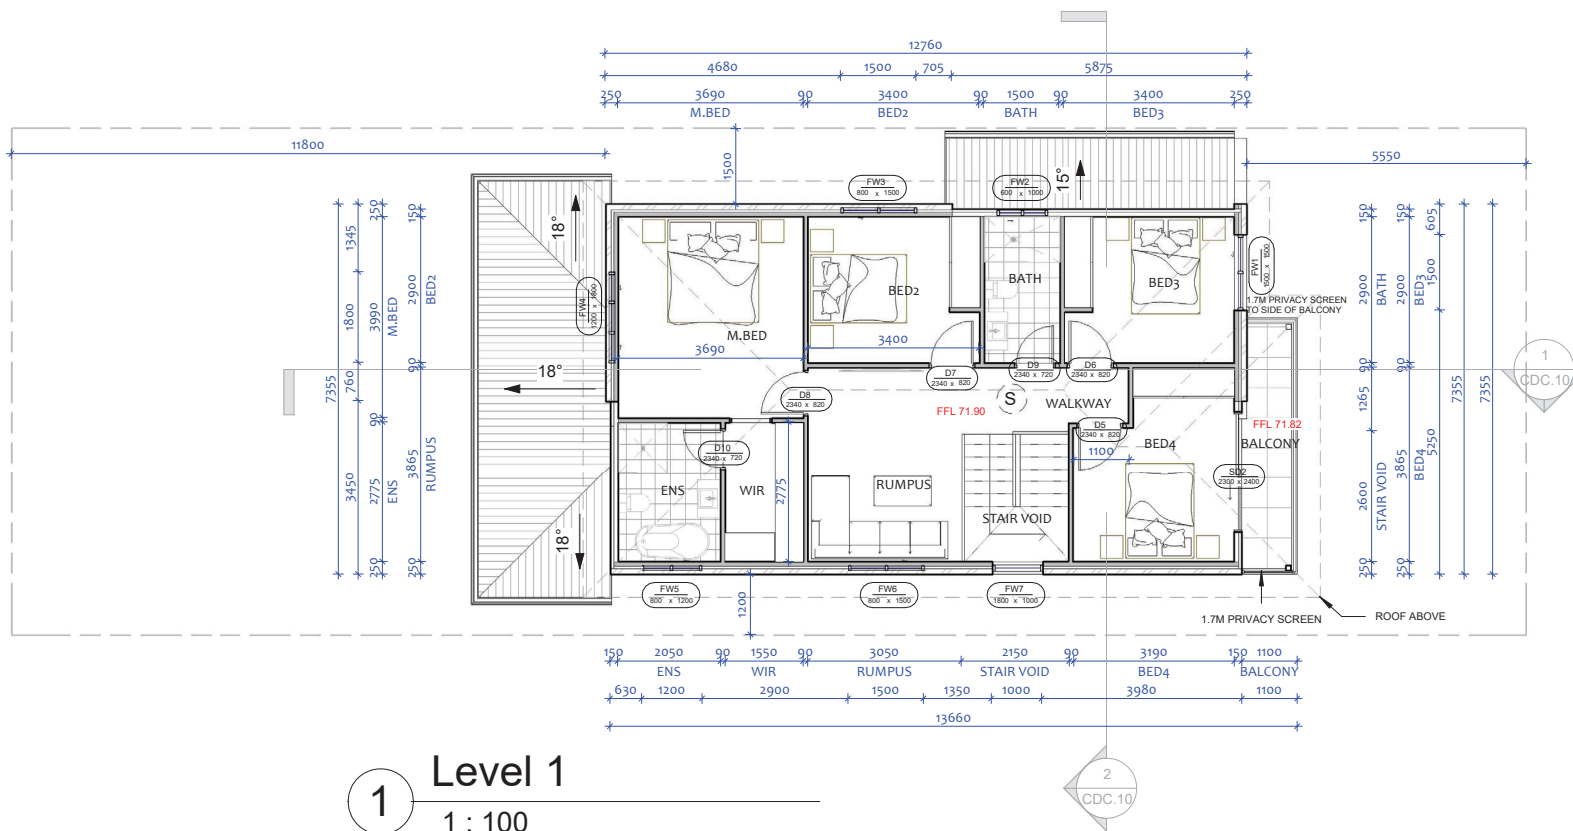

NOTE: PLEASE REFER TO TENDER FOR ALL INCLUSIONS.

REV	DATE	DESCRIPTION	BY
2	02-07-2026	Balcony added and Plan and Facade updated accordingly - Ekta/Biswash	
1	30-06-2026	CDC ISSUE	



RUBY HOMES

THIS DRAWING IS THE EXCLUSIVE PROPERTY OF THE DEVELOPER & THE REPRODUCTION OF ANY PART WITHOUT THE PRIOR WRITTEN CONSENT OF THE DEVELOPER IS A VIOLATION OF APPLICABLE LAWS. IN NO EVENT SHALL THE DEVELOPER BE HELD LIABLE FOR SPECIAL COLLATERAL INCIDENTAL OR CONSEQUENTIAL LIABILITY IN CONNECTION WITH THE USE OF THIS DIGITAL DATA ONCE RELEASED FROM THE DEVELOPER'S OFFICE. THIS DRAWING IS TO BE READ & UNDERSTOOD IN CONJUNCTION WITH THE STRUCTURAL, MECHANICAL, ELECTRICAL & / OR ANY OTHER CONSULTANT'S DOCUMENTATION AS MAY BE APPLICABLE TO THE PROJECT PRIOR TO THE START OF ANY WORKS AND FOR ITS DURATION.

PROJECT: Lot 11 11 SOLSTICE STREET 11 SOLSTICE STREET AUSTRAL	DRAWING TITLE: FIRST FLOOR LEVEL	NORTH: 	LOT NO: 11	DATE: 20-07-2026	SCALE: 1 : 100	DRAWING No: CDC.06	REV: 2
			DRAWN BY: AS	CHECKED BY: RH			ISSUED BY:
			DRAFTED BY: SL	CLIENT NAME: Owner			

OnBuild Construction Ltd
Reference: 2026/07/06
Date: 20-07-2026
Andrew Selman
Director/ Principal Designer
BPC 3541
Consultant who prepared this document
remains responsible for accuracy

IMPORTANT NOTES:
ALL DIMENSIONS AND NOTES ON ALL PLANS MUST BE CHECKED
AND VERIFIED BY BUILDERS AND OWNER PRIOR TO
COMMENCEMENT OF ANY BUILDING WORKS. TO CLARIFY AND
CONFIRM WITH CONSTRUCTION COMPANY FOR DISCREPANCIES
ON ALL DOCUMENTS AND PLANS PROVIDED FOR
CONSTRUCTION. ANY WORK INDICATED ON THE PLAN BUT NOT IN
CONTRACT, VARIATION TO PLANS SPECIFICATIONS MAY NOT BE
RESPONSIBILITY OF THE BUILDER. END USER TO VERIFY PLANS
CURRENT BCA AND AUSTRALIAN STANDARDS.
WINDOWS TO COMPLY WITH 3.9.3.5 OF THE BCA.

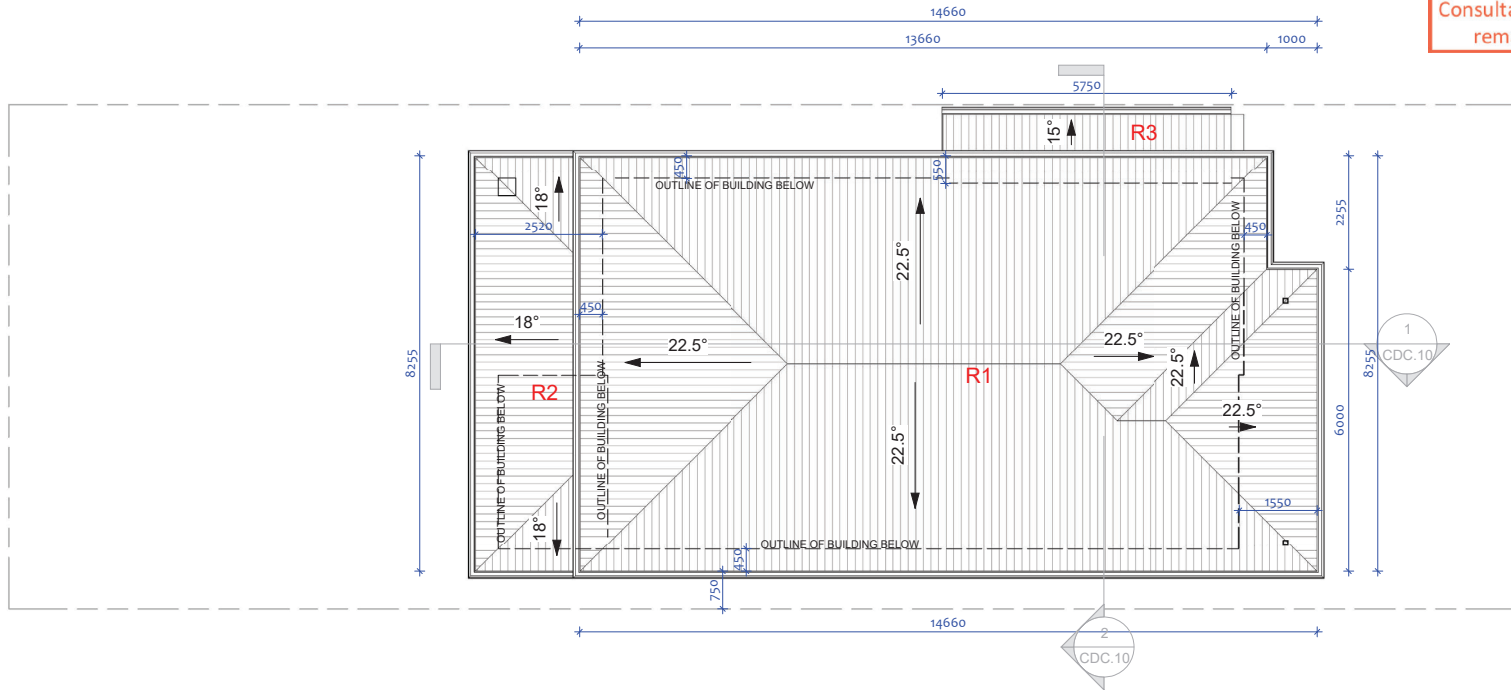

1 ROOF PLAN
1 : 100

Roof Schedule			
Mark	Base Level	Area	Comments
R2	Ground Ceiling	23 m ²	COLORBOND
R3	Ground Ceiling	9 m ²	COLORBOND
Ground Ceiling: 2		31 m ²	
R1	CEILING LEVEL	129 m ²	COLORBOND
CEILING LEVEL: 1		129 m ²	
Grand total: 3		160 m ²	

REV	DATE	DESCRIPTION	BY
2	02-07-2026	Balcony added and Plan and Facade updated accordingly - Eka/Biswash	
1	30-06-2026	CDC ISSUE	




RUBY HOMES


THIS DRAWING IS THE EXCLUSIVE PROPERTY OF THE DEVELOPER & THE REPRODUCTION OF ANY PART WITHOUT THE PRIOR WRITTEN CONSENT OF THE DEVELOPER IS A VIOLATION OF APPLICABLE LAWS. IN NO EVENT SHALL THE DEVELOPER BE HELD LIABLE FOR SPECIAL COLLATERAL, INCIDENTAL OR CONSEQUENTIAL LIABILITY IN CONNECTION WITH THE USE OF THIS DIGITAL DATA ONCE RELEASED FROM THE DEVELOPER'S OFFICE. THIS DRAWING IS TO BE READ & UNDERSTOOD IN CONJUNCTION WITH THE STRUCTURAL, MECHANICAL, ELECTRICAL &/ OR ANY OTHER CONSULTANT'S DOCUMENTATION AS MAY BE APPLICABLE TO THE PROJECT PRIOR TO THE START OF ANY WORKS AND FOR ITS DURATION.

PROJECT:
Lot 11 11 SOLSTICE STREET
11 SOLSTICE STREET AUSTRAL


DRAWING TITLE:
ROOF PLAN

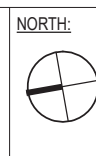

LOT NO:	DATE:	SCALE:	DRAWING No:	REV:
11	20-07-2026	1 : 100	CDC.07	2
DRAWN BY:	CHECKED BY:	CLIENT NAME:	ISSUED BY:	
AS	RH	Owner		
DRAFTED BY:				
SL				

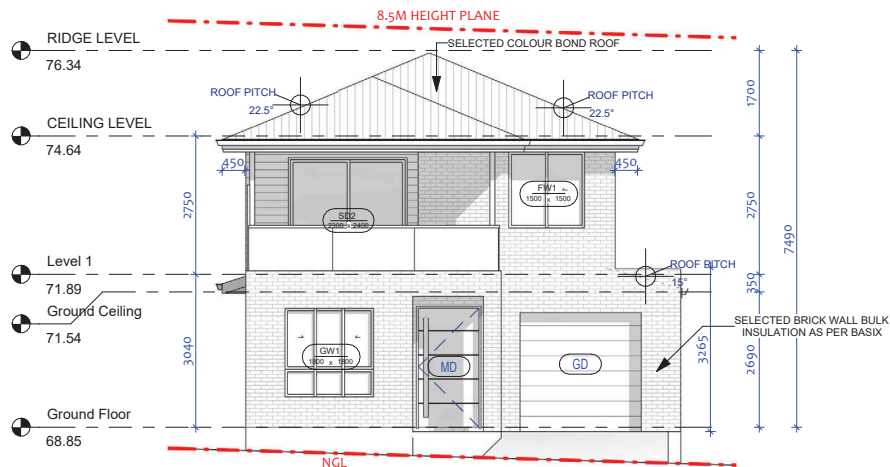

1 SOUTH ELEVATION
1 : 100

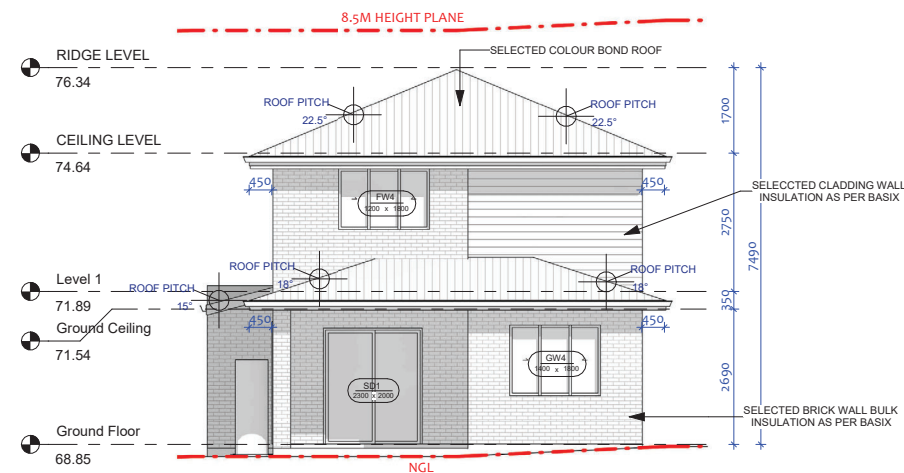

2 NORTH ELEVATION
1 : 100

OnBuild Certifiers Pty Ltd
Reference: 260050
Date: 27/07/2026
Andrew Soliman
Director / Principal Certifier
BDC2940
Consultant who prepared this document
remains responsible for accuracy

Mark	Height	Width	Sill Height	Head Height	Description
------	--------	-------	-------------	-------------	-------------

Ground Floor

GW1	1800	1800	600	2400	SLIDING & FIXED
GW2	600	900	1800	2400	SLIDING
GW3	600	1800	1050	1650	FIXED
GW4	1400	1800	1000	2400	SLIDING
GW5	1500	1000	900	2400	SLIDING

Ground Floor: 5

Level 1

FW1	1500	1500	950	2450	SLIDING
FW2	600	1000	1850	2450	SLIDING
FW3	800	1500	1650	2450	SLIDING
FW4	1200	1800	1250	2450	SLIDING
FW5	800	1200	1650	2450	SLIDING
FW6	800	1500	1650	2450	SLIDING
FW7	1800	1000	650	2450	FIXED

Level 1: 7

Mark	Height	Width	Count	Description
------	--------	-------	-------	-------------

Ground Floor

D1	2340	820	1	FLUSH DOOR
D2	2340	720	1	FLUSH DOOR
D3	2340	720	1	FLUSH DOOR
D4	2340	720	1	FLUSH DOOR
GD	2400	2400	1	GARAGE DOOR
MD	2400	1200	1	SOLID CORE DOOR
SD1	2300	2000	1	SLIDING DOOR

Ground Floor: 7

Level 1

D5	2340	820	1	FLUSH DOOR
D6	2340	820	1	FLUSH DOOR
D7	2340	820	1	FLUSH DOOR
D8	2340	820	1	FLUSH DOOR
D9	2340	720	1	FLUSH DOOR
D10	2340	720	1	FLUSH DOOR
SD2	2300	2400	1	SLIDING DOOR

Level 1: 7

REV	DATE	DESCRIPTION	BY
2	02-07-2026	Balcony added and Plan and Facade updated accordingly - Ekta/Biswash	
1	30-06-2026	CDC ISSUE	

RUBY HOMES

THIS DRAWING IS THE EXCLUSIVE PROPERTY OF THE DEVELOPER & THE REPRODUCTION OF ANY PART WITHOUT THE PRIOR WRITTEN CONSENT OF THE DEVELOPER IS A VIOLATION OF APPLICABLE LAWS. IN NO EVENT SHALL THE DEVELOPER BE HELD LIABLE FOR SPECIAL, COLLATERAL, INCIDENTAL OR CONSEQUENTIAL LIABILITY IN CONNECTION WITH THE USE OF THIS DIGITAL DATA ONCE RELEASED FROM THE DEVELOPERS OFFICE. THIS DRAWING IS TO BE READ & UNDERSTOOD IN CONJUNCTION WITH THE STRUCTURAL, MECHANICAL, ELECTRICAL & / OR ANY OTHER CONSULTANT'S DOCUMENTATION AS MAY BE APPLICABLE TO THE PROJECT PRIOR TO THE START OF ANY WORKS AND FOR ITS DURATION.

PROJECT:
Lot 11 11 SOLSTICE STREET
11 SOLSTICE STREET AUSTRAL


DRAWING TITLE:
ELEVATION 01

NORTH:


LOT NO:	DATE:	SCALE:	DRAWING No:	REV:
11	20-07-2026	1 : 100	CDC.08	2
DRAWN BY:	CHECKED BY:	CLIENT NAME:	ISSUED BY:	
AS	RH	Owner		
DRAFTED BY:				
SL				

CDC ISSUE

OnBuild Certifiers Pty Ltd
Reference: 260050
Date: 27/07/2026
Andrew Soliman
Director/ Principal Certifier
BDC2940
Consultant who prepared this document
remains responsible for accuracy

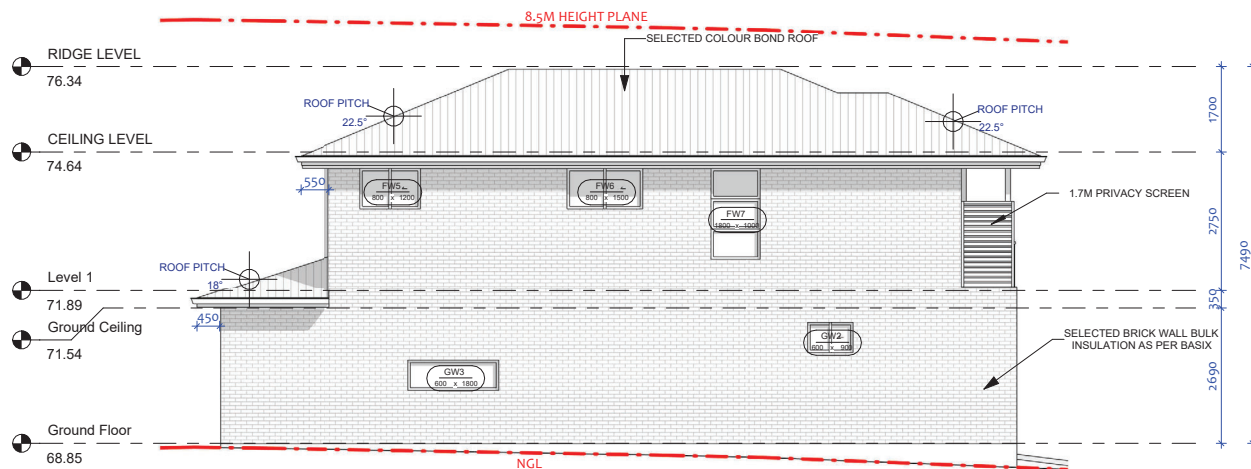

1 WEST ELEVATION
1 : 100

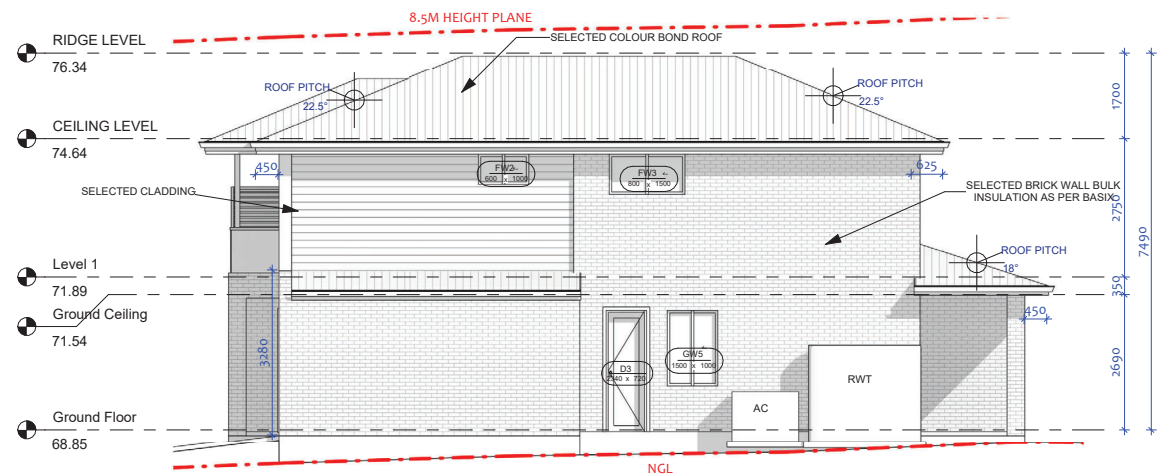

2 EAST ELEVATION
1 : 100

REV	DATE	DESCRIPTION	BY
2	02-07-2026	Balcony added and Plan and Facade updated accordingly - Ekta/Biswash	
1	30-06-2026	CDC ISSUE	

RUBY HOMES

THIS DRAWING IS THE EXCLUSIVE PROPERTY OF THE DEVELOPER & THE REPRODUCTION OF ANY PART WITHOUT THE PRIOR WRITTEN CONSENT OF THE DEVELOPER IS A VIOLATION OF APPLICABLE LAWS. IN NO EVENT SHALL THE DEVELOPER BE HELD LIABLE FOR SPECIAL COLLATERAL, INCIDENTAL OR CONSEQUENTIAL LIABILITY IN CONNECTION WITH THE USE OF THIS DIGITAL DATA ONCE RELEASED FROM THE DEVELOPER'S OFFICE. THIS DRAWING IS TO BE READ & UNDERSTOOD IN CONJUNCTION WITH THE STRUCTURAL, MECHANICAL, ELECTRICAL &/OR ANY OTHER CONSULTANT'S DOCUMENTATION AS MAY BE APPLICABLE TO THE PROJECT PRIOR TO THE START OF ANY WORKS AND FOR ITS DURATION.

PROJECT:
**Lot 11 11 SOLSTICE STREET
11 SOLSTICE STREET
AUSTRAL**

DRAWING TITLE:
ELEVATION 02

NORTH:

LOT NO:

11

DRAWN BY:

AS

DRAFTED BY:

SL

DATE:

20-07-2026

CHECKED BY:

RH

CLIENT NAME:

Owner

SCALE:

1 : 100

DRAWING No:

CDC.09

REV:

2

CDC ISSUE

ISSUED BY:

Architectural section drawing of a two-story house. The drawing shows the internal layout including a walkway, bedroom (BED3), hallway, and garage. Key levels are marked on the left: Ridge Level (76.34), Ceiling Level (74.64), Level 1 (71.89), Ground Ceiling (71.54), and Ground Floor (68.85). The roof is labeled "8.5M HEIGHT LIMIT (MAX)" and "SELECTED COLOUR BOND ROOF". The roof structure is shown with insulation and plasterboard. The walls are labeled "SELECTED BRICK WALL BULK INSULATION AS PER BASIX". The floor is labeled "TIMBER FLOOR". The drawing includes dimensions for the roof pitch (22.5°), ceiling height (2750), and floor height (2690).

Architectural section drawing of a two-story house. The drawing shows the internal layout and structural details. Key features include:

- Roof:** Ridge level at 76.34, roof insulation as per basis, selected colour bond roof, roof pitch of 22.5°.
- First Floor:** Ceiling level at 74.64, rooms include BED4, WALKWAY, RUMPUS, and M.BED. A balcony is located on the left side.
- Ground Floor:** Level 1 at 71.89, ground ceiling at 71.54, rooms include PORCH, HALLWAY, LIVING, and ALFRESCO. A selected brick wall bulk insulation as per basis is shown on the right.
- Ground Floor Level:** 68.85, NGL (Natural Ground Level) is indicated.
- Dimensions:** Total height from ground level to ridge is 8.5m (MAX). Vertical dimensions on the right indicate floor-to-floor heights of 2750mm and 2690mm, and a total height of 7490mm.

1	30-06-2026	CDC ISSUE	
REV	DATE	DESCRIPTION	BY



THIS DRAWING IS THE EXCLUSIVE PROPERTY OF THE DEVELOPER & THE REPRODUCTION OF ANY PART WITHOUT THE PRIOR WRITTEN CONSENT OF THE DEVELOPER IS A VIOLATION OF APPLICABLE LAWS. IN NO EVENT SHALL THE DEVELOPER BE HELD LIABLE FOR SPECIAL COLLATERAL, INCIDENTAL OR CONSEQUENTIAL LIABILITY IN CONNECTION WITH THE USE OF THIS DIGITAL DATA ONCE RELEASED FROM THE DEVELOPER'S OFFICE. THIS DRAWING IS TO BE READ & UNDERSTOOD IN CONJUNCTION WITH THE STRUCTURAL, MECHANICAL, ELECTRICAL & / OR ANY OTHER CONSULTANT DOCUMENTATION AS MAY BE APPLICABLE TO THE PROJECT PRIOR TO THE START OF ANY WORKS AND BEFORE ITS DURATION.

DRAWING TITLE:

SECTIONS

	<u>NORTH:</u>
--	---------------

LOT NO:

DATE:	20-07-2026
-------	------------

SCALE:

CDC ISSUE

1

CDC 10


ISSUED BY:

DRAWN BY:

	CHECKED BY:
--	-------------


DRAFTED BY
SL

CLIENT NAME	Owner
-------------	-------

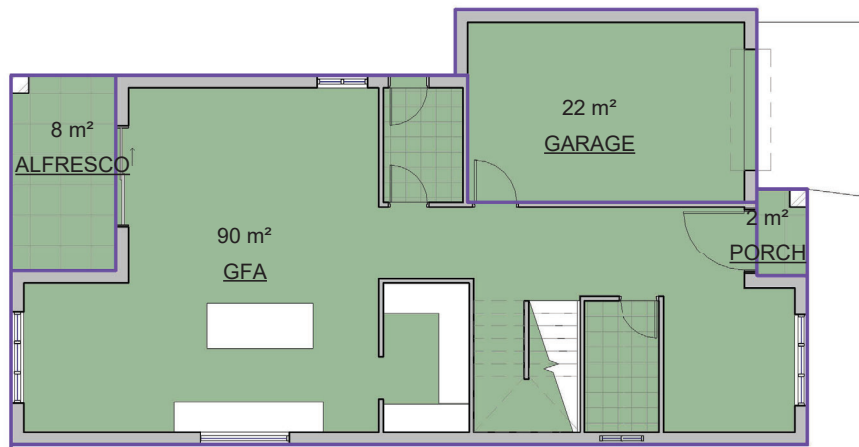

1 Ground Floor
1 : 100

OnBuild Certifiers Pty Ltd	
Reference: 260050	
Date: 27/07/2026	
Area Schedule (Gross Building)	
Director/ Principal Certifier	Name
BDC2940	Andrew Schman
Consultant who prepared this document remains responsible for accuracy	
Ground Floor	
GARAGE	22 m²
PORCH	2 m²
ALFRESCO	8 m²
GFA	90 m²
Ground Floor: 4	122 m²
Level 1	
FFA	93 m²
STAIR VOID	6 m²
Level 1: 2	99 m²
Grand total: 6	221 m²

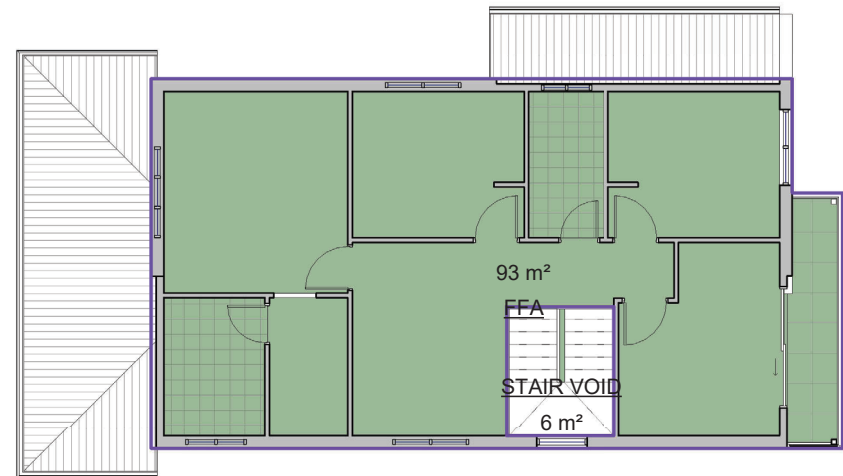

2 Level 1
1 : 100

REV	DATE	DESCRIPTION	BY
2	02-07-2026	Balcony added and Plan and Facade updated accordingly - Eka/Biswash	
1	30-06-2026	CDC ISSUE	

RUBY HOMES

THIS DRAWING IS THE EXCLUSIVE PROPERTY OF THE DEVELOPER & THE REPRODUCTION OF ANY PART WITHOUT THE PRIOR WRITTEN CONSENT OF THE DEVELOPER IS A VIOLATION OF APPLICABLE LAWS. IN NO EVENT SHALL THE DEVELOPER BE HELD LIABLE FOR SPECIAL, COLLATERAL, INCIDENTAL OR CONSEQUENTIAL LIABILITY IN CONNECTION WITH THE USE OF THIS DIGITAL DATA ONCE RELEASED FROM THE DEVELOPER'S OFFICE. THIS DRAWING IS TO BE READ & UNDERSTOOD IN CONJUNCTION WITH THE STRUCTURAL, MECHANICAL, ELECTRICAL & / OR ANY OTHER CONSULTANT'S DOCUMENTATION AS MAY BE APPLICABLE TO THE PROJECT PRIOR TO THE START OF ANY WORKS AND FOR ITS DURATION.

PROJECT:
Lot 11 11 SOLSTICE STREET
11 SOLSTICE STREET
AUSTRAL

DRAWING TITLE:
FLOOR AREA PLAN




LOT NO:
11
DRAWN BY:
AS
CHECKED BY:
RH
DRAFTED BY:
SL


DATE:
20-07-2026
SCALE:
1 : 100
CLIENT NAME:
Owner

CDC ISSUE

DRAWING No:
CDC.11
REV:
2
ISSUED BY:

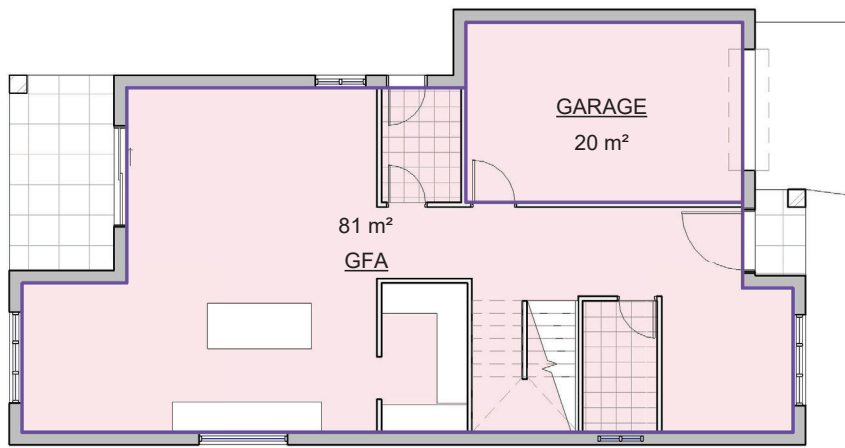

1 Ground Floor
1 : 100

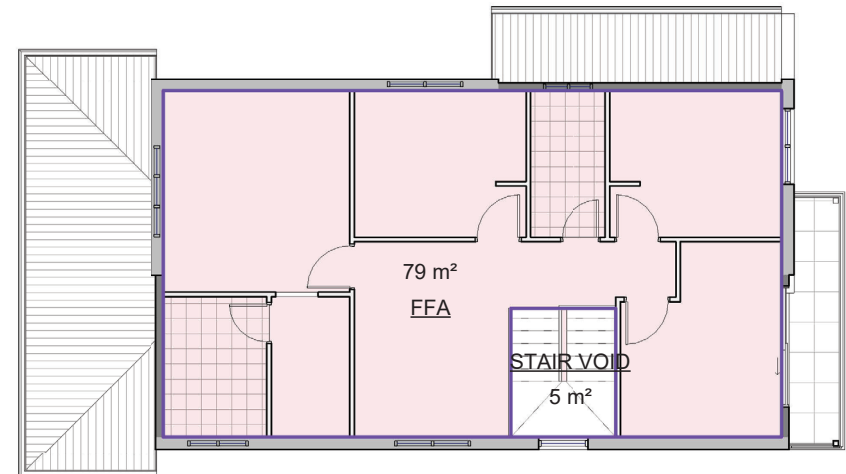

2 Level 1
1 : 100

OnBuild Certifiers Pty Ltd
Reference: 260050
Date: 27/07/2026
Andrew Soliman
Director/ Principal Certifier
BDC1212

Area Schedule (Rentable)
NameArea
Consultant who prepared this document remains responsible for accuracy

GFA	81 m ²
GARAGE	20 m ²
Ground Floor: 2	100 m ²
Level 1	
FFA	79 m ²
STAIR VOID	5 m ²
Level 1: 2	84 m ²
Grand total: 4	184 m ²

1	30-06-2026	CDC ISSUE	
REV	DATE	DESCRIPTION	BY

THIS DRAWING IS THE EXCLUSIVE PROPERTY OF THE DEVELOPER & THE REPRODUCTION OF ANY PART WITHOUT THE PRIOR WRITTEN CONSENT OF THE DEVELOPER IS A VIOLATION OF APPLICABLE LAWS. IN NO EVENT SHALL THE DEVELOPER BE HELD LIABLE FOR SPECIAL, COLLATERAL, INCIDENTAL OR CONSEQUENTIAL LIABILITY IN CONNECTION WITH THE USE OF THIS DIGITAL DATA ONCE RELEASED FROM THE DEVELOPER'S OFFICE. THIS DRAWING IS TO BE READ & UNDERSTOOD IN CONJUNCTION WITH THE STRUCTURAL, MECHANICAL, ELECTRICAL & / OR ANY OTHER CONSULTANT'S DOCUMENTATION AS MAY BE APPLICABLE TO THE PROJECT PRIOR TO THE START OF ANY WORKS AND FOR ITS DURATION.

PROJECT:
Lot 11 11 SOLSTICE STREET
11 SOLSTICE STREET
AUSTRAL

DRAWING TITLE:
RENTABLE AREA PLAN

NORTH:

LOT NO:
11
 DRAWN BY:
AS
 CHECKED BY:
RH
 DRAFTED BY:
SL

DATE:
20-07-2026
 SCALE:
1 : 100
 CLIENT NAME:
Owner

DRAWING No.	REV.
CDC.12	1
	ISSUED BY:

OnBuild Certifiers Pty Ltd
Reference: 260050
Date: 27/07/2026
Andrew Soliman
Director/ Principal Certifier
BDC2940
Consultant who prepared this document
remains responsible for accuracy



	1. RF	2. BR1	3. CD1	4. AL	5. ED	6. GD	7. FAS	8. GUT
	ROOF	MAIN WALLS	CLADDING	WINDOWS/ BALUSTRADE	MAIN DOOR	GARAGE DOOR	FASCIA	GUTTER
MATERIAL	COLORBOND DARK MONUMENT	BRICK	BLUEBOARD	ALUMINIUM	TIMBER	COLORBOND	COLORBOND	COLORBOND
COLOUR								

NOTE : ALL COLOURS SPECIFIED ARE INDICATIVE ONLY AND ARE SUBJECT TO VARIATION AND TO AVAILABILITY
ANY DISCREPANCY PLEASE FOLLOW AS PER RENDERED IMAGE

REV	DATE	DESCRIPTION	BY
1	30-06-2026	CDC ISSUE	



RUBY
HOMES

THIS DRAWING IS THE EXCLUSIVE PROPERTY OF THE DEVELOPER & THE REPRODUCTION OF ANY PART WITHOUT THE PRIOR WRITTEN CONSENT OF THE DEVELOPER IS A VIOLATION OF APPLICABLE LAWS. IN NO EVENT SHALL THE DEVELOPER BE HELD LIABLE FOR SPECIAL, COLLATERAL, INCIDENTAL OR CONSEQUENTIAL LIABILITY IN CONNECTION WITH THE USE OF THIS DIGITAL DATA ONCE RELEASED FROM THE DEVELOPER'S OFFICE. THIS DRAWING IS TO BE READ & UNDERSTOOD IN CONJUNCTION WITH THE STRUCTURAL, MECHANICAL, ELECTRICAL & / OR ANY OTHER CONSULTANT'S DOCUMENTATION AS MAY BE APPLICABLE TO THE PROJECT PRIOR TO THE START OF ANY WORKS AND FOR ITS DURATION.


PROJECT:
**Lot 11 11 SOLSTICE STREET
11 SOLSTICE STREET
AUSTRAL**

DRAWING TITLE:
COLOR SCHEDULE

NORTH:

LOT NO:	DATE:	SCALE:	DRAWING No:	REV:
11	20-07-2026	1 : 100	CDC.14	1
DRAWN BY:	CHECKED BY:			ISSUED BY:
AS	RH			
DRAFTED BY:	CLIENT NAME:			
SL	Owner			

OnBuild Certifiers Pty Ltd
Reference: 260050
Date: 27/07/2026
Andrew Soliman
Director/ Principal Certifier
BDC2940
Consultant who prepared this document
remains responsible for accuracy

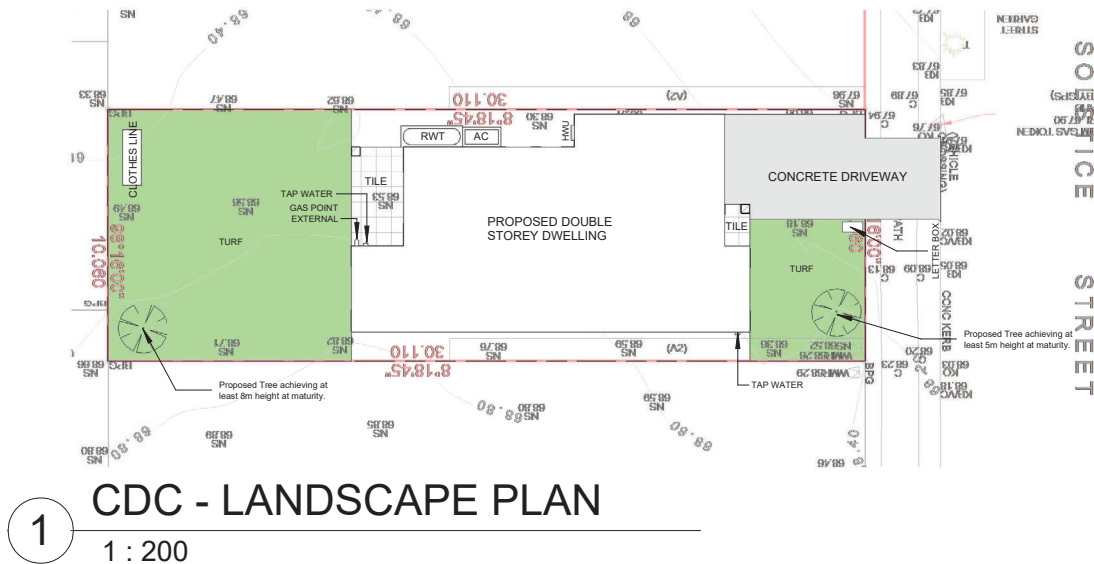

GENERAL NOTES:

- LANDSCAPE CONTRACTOR TO CHECK DA CONDITIONS AND STAMPED LANDSCAPE PLAN.
- BEFORE COMMENCING WORKS TO ENSURE NO ADDITIONS/AMENDMENTS TO PLAN.
- GARDEN BEDS IN OSD BASIN TO CONSIST OF NON FLOATABLE DECORATIVE GRAVEL.
- REFER TO HYDRAULICS ENGINEERS PLAN FOR OSD DETAILS/FINAL LEVELS.
- MULCHED PLANTING BEDS TO BE A MINIMUM DEPTH OF 75mm AS SELECTED.
- CONTRACTOR'S RESPONSIBILITY TO CHECK AND ADJUST SOIL pH AS REQUIRED.
- PROVIDE TIMBER EDGE AS A MINIMUM BENEATH FENCING/GATES TO DEFINE TURF AND GARDEN BEDS/PATHWAYS. EDGING TO BE PROVIDED TO ALL AREAS WHERE DIFFERING MATERIALS MEET i.e. TURF/GARDEN, TURF/GRAVEL PATH ETC.
- WEED MAT BENEATH GRAVEL PATHWAYS REQUIRED TO LIMIT MUD TRACKING.
- PREMIUM ORGANIC GARDEN MIX TO BE USED.
- ALL PLANTS TO BE HEALTHY AND VIGOROUS.
- CONTRACTOR TO MAKE GOOD TURF ON NATURE STRIP POST CONSTRUCTION.
- CONTRACTOR TO MAKE GOOD TURF ON NATURE STRIP POST CONSTRUCTION.
- DO NOT SCALE ARCHITECTURAL SETOUT FROM LANDSCAPE DRAWING.
- EXISTING TREE SPREAD APPROXIMATE ONLY. REFER TO TREE REPORT WHEN APPLICABLE.
- SITE SURVEY PROVIDED BY OTHERS.
- BUFFALO TURF PREFERRED OVER KIKUYU.

LANDSCAPE BASIX NOTE:

THE APPLICANT MUST PLANT INDIGENEOUS OR LOW WATER USE SPECIES OF VEGETATION THROUGHOUT 15 SQM OF THE SITE.

NOTE: BUILDER RESERVES THE RIGHT NOT TO UNDERTAKE NOR SUPPLY CERTIFICATE FOR OCCUPATION CERTIFICATE.


NOTE: TO AID COMPLIANCE WITH BASIX LEGISLATION, PLANTS (WHERE APPLICABLE) HAVE BEEN SELECTED FROM THE LOCAL CITY COUNCIL SHIRE PLANT LISTS.

NOTE: LOCATION OF SEWER MAINS, LINES, WATER PIPES, UNDERGROUND ELECTRICITY AND OTHER SERVICES MUST BE OBTAINED PRIOR TO COMMENCEMENT OF ANY WORK ON SITE.

CONTRACTORS NOTE: CALCULATED AREAS DETERMINED BY CAD AND HAVE BEEN ROUNDED UP FOR USE AS A GUIDE ONLY. ALLOW STANDARD PERCENTAGE FOR CUTTING AND WASTAGE. CONFIRM DIMENSIONS AND NUMBERS PRIOR TO QUOTING/ORDERING.


LANDSCAPE AREA

FRONT AREA	25.9 m ²
BACKYARD AREA	97.8 m ²
TOTAL	122.7 m ²

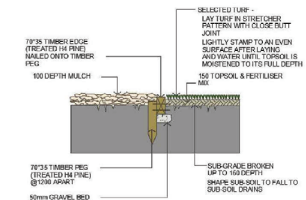

1. TURF & GARDEN EDGE DETAIL

NOTE:
ALIGNMENT OF BRICK EDGE SHALL BE EVEN & FREE FROM SPLITS AND HUMPS.

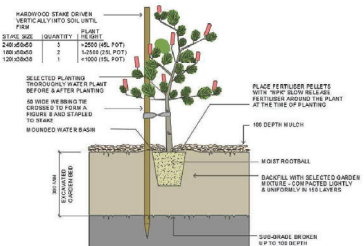

2. TREE & SHRUB PLANTING IN GARDEN BED

NOTE:
DO NOT PLANT IN UNSUITABLE WEATHER CONDITIONS
DO NOT PLANT IN EXTREME HEAT, COOL WITH 50mm
CLAY SOIL IS TO BE TREATED WITH CLAY BREAKER
AND ORGANIC COMPOST

REV	DATE	DESCRIPTION	BY
1	30-06-2026	CDC ISSUE	

RUBY HOMES

THIS DRAWING IS THE EXCLUSIVE PROPERTY OF THE DEVELOPER & THE REPRODUCTION OF ANY PART WITHOUT THE PRIOR WRITTEN CONSENT OF THE DEVELOPER IS A VIOLATION OF APPLICABLE LAWS. IN NO EVENT SHALL THE DEVELOPER BE HELD LIABLE FOR SPECIAL, COLLATERAL, INCIDENTAL OR CONSEQUENTIAL LIABILITY IN CONNECTION WITH THE USE OF THIS DIGITAL DATA ONCE RELEASED FROM THE DEVELOPER'S OFFICE. THIS DRAWING IS TO BE READ & UNDERSTOOD IN CONJUNCTION WITH THE STRUCTURAL, MECHANICAL, ELECTRICAL &/OR ANY OTHER CONSULTANT'S DOCUMENTATION AS MAY BE APPLICABLE TO THE PROJECT PRIOR TO THE START OF ANY WORKS AND FOR ITS DURATION.

PROJECT:
**Lot 11 11 SOLSTICE STREET
11 SOLSTICE STREET
AUSTRAL**

DRAWING TITLE:
LANDSCAPE PLAN



LOT NO:	DATE:	SCALE:	DRAWING No:	REV:
11	20-07-2026	1 : 200	CDC.15	1
DRAWN BY:	CHECKED BY:		ISSUED BY:	
AS	RH			
DRAFTED BY:	CLIENT NAME:			
SL	Owner			

ABCB HOUSING PROVISIONS : PART 10.2 WET AREA WATERPROOFING

10.2.1 Wet Areas

1. Building elements in wet areas within a building must be protected with a waterproofing system.
2. The waterproofing system in (1) must be either waterproof or water resistant in accordance with 10.2.2 to 10.2.6.

10.2.2 Shower Area (enclosed and unenclosed)

1. For a shower area with a hob, step-down or level threshold, the following applies:
a. The floor of the shower area must be waterproof, including any hob or step-down (see Figure 10.2.2); and
b. The walls of the shower area must be waterproof not less than 1800 mm above the floor substrate (see Figure 10.2.2).
c. Wall junctions and joints within the shower area must be waterproof not less than 40 mm either side of the junction (see Figure 10.2.2).
d. Wall/floor junctions within the shower area must be waterproof (see Figure 10.2.2).
e. Penetrations within the shower area must be waterproof.
2. A shower with a preformed shower base must also comply with the requirements of (1), except for (a) which is not applicable.

Figure 10.2.2: Extent of treatment for shower areas - concrete compressed fibre-cement and fibre-cement sheet floors.

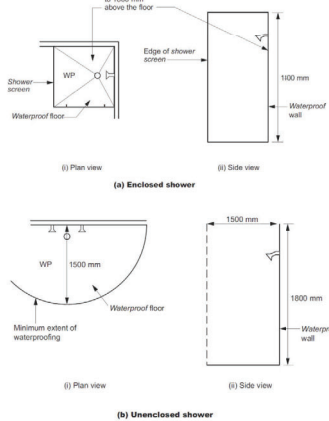


Figure Notes
Wall/floor junction heights are to be as per 10.2.2 to 10.2.6 (as applicable).

Notes
Where a shower is above a bath or spa, use requirements for shower.

10.2.3 Area outside shower area

1. For concrete, compressed fibre-cement and fibre-cement sheet flooring, the floor of the room must be water resistant.
2. For timber floors including particleboard, plywood and other timber based flooring materials, the floor of the room must be waterproof.
3. Wall/floor junctions must be -
a. waterproof, and
b. where a flashing is used, the horizontal leg must be not less than 40 mm.

10.2.4 Areas adjacent to baths and spas without showers

1. For areas adjacent to all baths and spas, the following applies:
a. For concrete, compressed fibre-cement and fibre-cement sheet flooring, the floor of the room must be water resistant.
b. For timber floors including particleboard, plywood and other timber based flooring materials, the floor of the room must be waterproof.
c. Tap and spout penetrations must be waterproof where they occur in horizontal surfaces.
2. For areas adjacent to non-freestanding baths and spas, the following applies:
a. Walls must be water resistant (see Figure 10.2.4a and Figure 10.2.4b).
b. To a height of not less than 150mm above the vessel, for the extent of the vessel, where the vessel is within 75mm of a wall and not within 40mm of a wall.
c. Wall junctions and joints must be water resistant within 150mm above a vessel for the extent of the vessel.
d. Wall/floor junctions must be waterproof for the extent of the vessel (see Figure 10.2.4a and Figure 10.2.4b).
3. For inserted baths and spas, the following applies:
a. For floors and horizontal surfaces:
i. Any shelf area adjoining the bath or spa must be waterproof and include a waterstop under the vessel lip.
ii. There are no requirements for the floor under a bath or spa.
b. For walls:
i. Waterproof to not less than 150mm above the lip of a bath or spa.
ii. There are no requirements for the floor under a bath or spa.
c. For wall junctions and joints, the following applies:
i. Waterproof junctions within 150mm of a bath or spa.
ii. There are no requirements for junctions and joints in walls beneath the lip of a bath or spa.
d. Tap and spout penetrations must be waterproof where they occur in horizontal surfaces.

Figure 10.2.4a: Areas adjacent to baths and spas without showers for concrete, compressed fibre-cement and fibre-cement sheet flooring




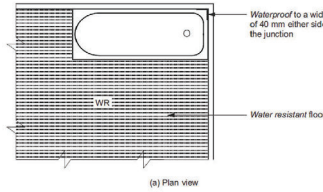



Figure 10.2.4b: Areas adjacent to baths and spas without showers for timber floors including particle-board, plywood and other floor materials

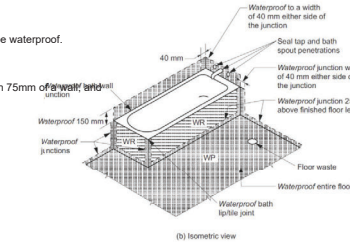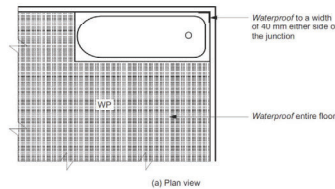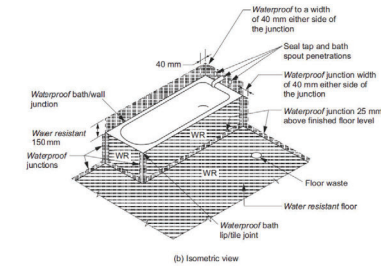

10.2.5 Other areas

1. For walls adjoining other types of vessels (not sink, bath or tub) (b), the following applies:
a. Walls must be water resistant to a height of not less than 150mm above the vessel, for the extent of the vessel, where the vessel is within 75 mm of a wall (see Figure 10.2.5).
b. Waterproof wall junctions must be water resistant.
c. Waterproof tap and spout penetrations where they occur in surfaces required to be waterproof or water resistant.
2. For laundries and WCs, the following applies:
a. The floor of the room must be water resistant.
b. Wall/floor junctions must be water resistant and where a flashing is used, the horizontal leg must be not less than 40 mm.
3. For WCs with a handheld bidet spray installation, the following applies:
a. The floor of the room must be waterproof.
b. Walls must be -
i. waterproof in WC area within a 900 mm radius from the wall connection of the handheld bidet spray device to a height of not less than 150mm above the floor substrate; and
ii. water resistant in WC area within a 900 mm radius from the wall connection of the handheld bidet device to not less than 1200 mm above the finished floor level of the WC.
c. Wall junctions within the WC area within 900 mm radius from the wall connection of the handheld bidet spray device must be waterproof.
d. Wall/floor junctions within the WC area within 1000 mm radius from the wall connection of the handheld bidet spray device must be waterproof.
e. Penetrations in the WC area must be waterproof.

Figure 10.2.5: Bath and vessel abutting wall - areas to be protected

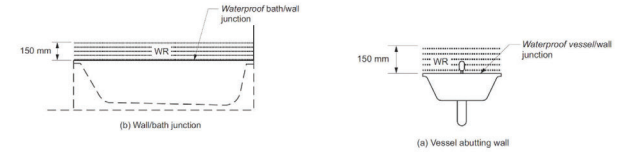

10.2.6 Waterproofing systems

1. For the purposes of this Part, a waterproofing system is deemed -
a. waterproof, if it complies with (2); or
b. water resistant, if it complies with (3).
2. For a waterproofing system required to be waterproof in accordance with 10.2.2 to 10.2.5, the materials nominated in 10.2.8 must be used.
3. For a waterproofing system required to be water resistant in accordance with 10.2.2 to 10.2.5, the materials nominated in 10.2.9 must be used in conjunction with the materials in 10.2.10.

10.2.12 Construction of wet area floors - falls

- Where a floor waste is installed -
a. the minimum continuous fall of a floor plane to the waste must be 1:80; and
b. the maximum continuous fall of a floor plane to the waste must be 1:50.

REV	DATE	DESCRIPTION	BY
1	30-06-2026	CDC ISSUE	



PROJECT:
Lot 11 11 SOLSTICE STREET
11 SOLSTICE STREET
AUSTRAL

DRAWING TITLE:
WATERPROOFING
DETAILS

NORTH:

LOT NO:	DATE:	SCALE:	DRAWING No:	REV:
11	20-07-2026	1 : 50	CDC.16	1
DRAWN BY:	CHECKED BY:	CLIENT NAME:	ISSUED BY:	
AS	RH	Owner		
DRAFTED BY:				
SL				