

PROPOSED SINGLE STOREY DWELLING
#12, Summer Street, Austral

PARAGON

Paragon Building Certifiers Pty Ltd

RBC00045

Registered Certifier

APPROVED

Reference: 260335/01

Date: 16/07/2026



Page No	Title
1	Coverpage
2	Safety in Design Notes
3	Building Specification
4	Building Specification
5	Basix Notes
6	Cut and Fill Plan
7	Slab Plan
8	Site Plan
9	Ground Floor Plan
10	Roof Plan
11	Elevation
12	Side Elevation
13	Section
14	Door Schedule & SOF
15	Window Schedule
16	Landscape Plan
17	Sediment Control Plan
18	GFA Calculation
19	Floor Finish

National Construction Code - Volume 2 Amendment 2 - Building Code of Australia 2022 & Housing Provisions Standard 2022

DRAWN BY: N.B	DATE : 01-07-2026	PROJECT NO. 2605 910
SCALE:	APPLICATION : CDC	ISSUE A
PAGE SIZE A3	PAGE NO: 2	

TERMITE SHEET

-TERMITE SHEET EXTENDS THROUGH THE ENTIRE MASONRY LEAF AND IS
VISIBLE AT THE FINISHED FACE OF THE WALL.

Figure 10.2.29 Typical membrane termination at drainage outlet




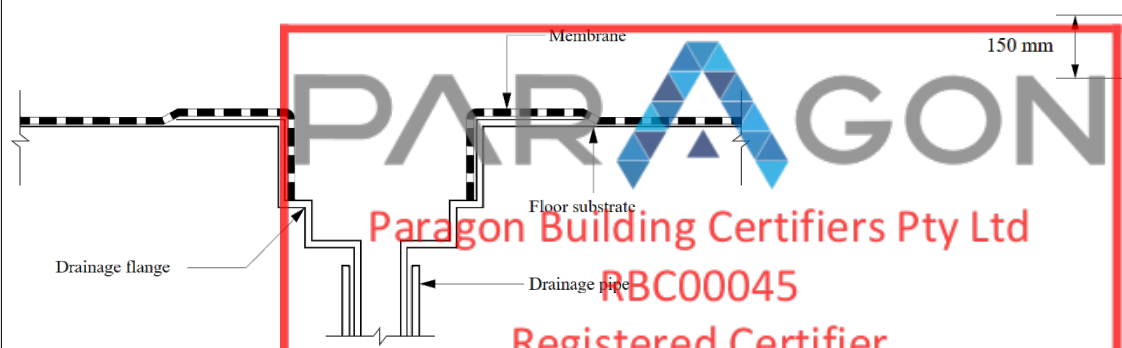


Figure 10.2.24 Typical bathroom door details for whole bathroom waterproofing

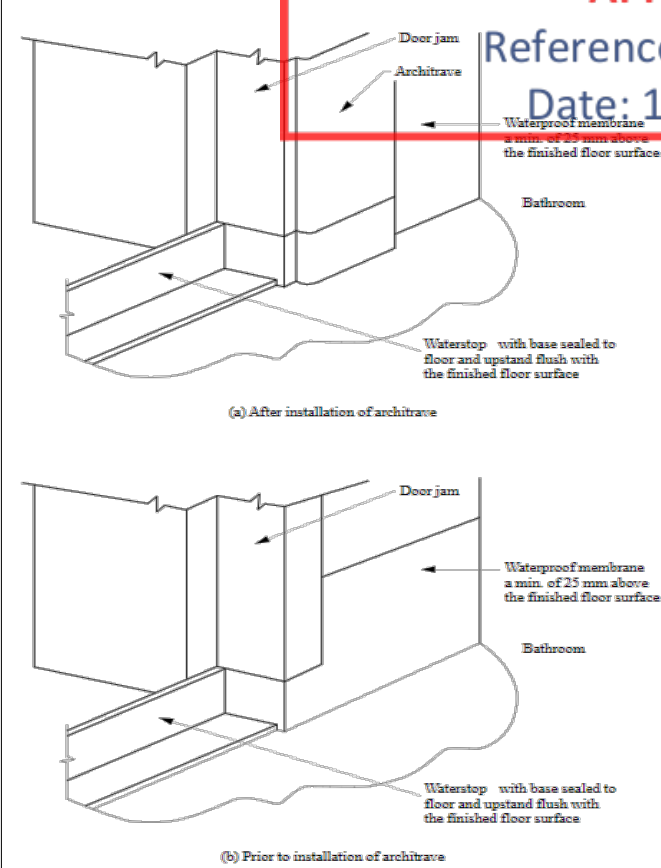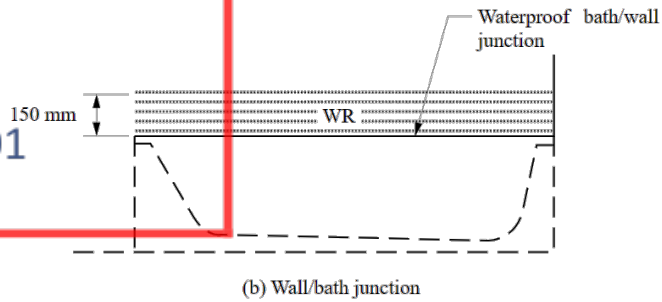

BASIN & BATHTUB:

Figure 10.2.5 Bath and vessel abutting wall — areas to be protected

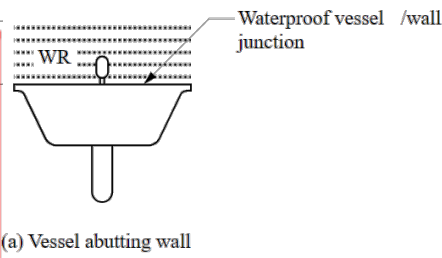

ENCLOSED SHOWER AREA

Figure 10.2.17 Typical hobless construction



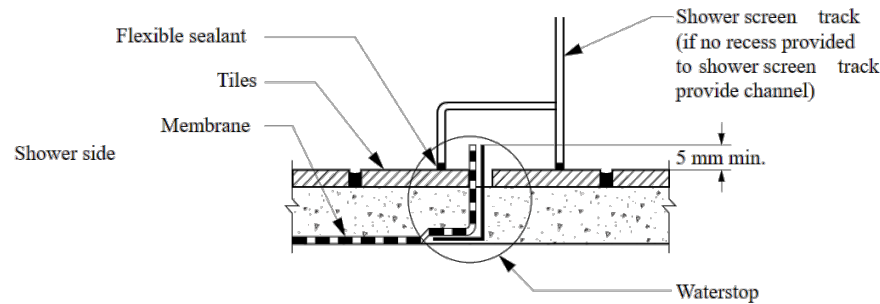


Figure 10.2.16: Typical hob construction — internal membrane

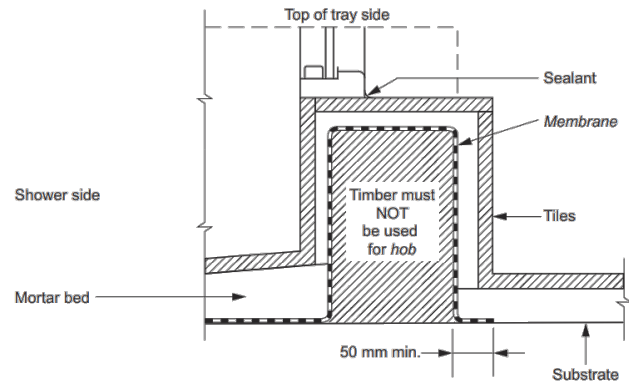

Typical detail of HOB Construction as per BCA ABCB Housing Provisions Part 10.2.16

Figure 10.2.2 Extent of treatment for shower areas — concrete compressed fibre-cement and fibre-cement sheet floors

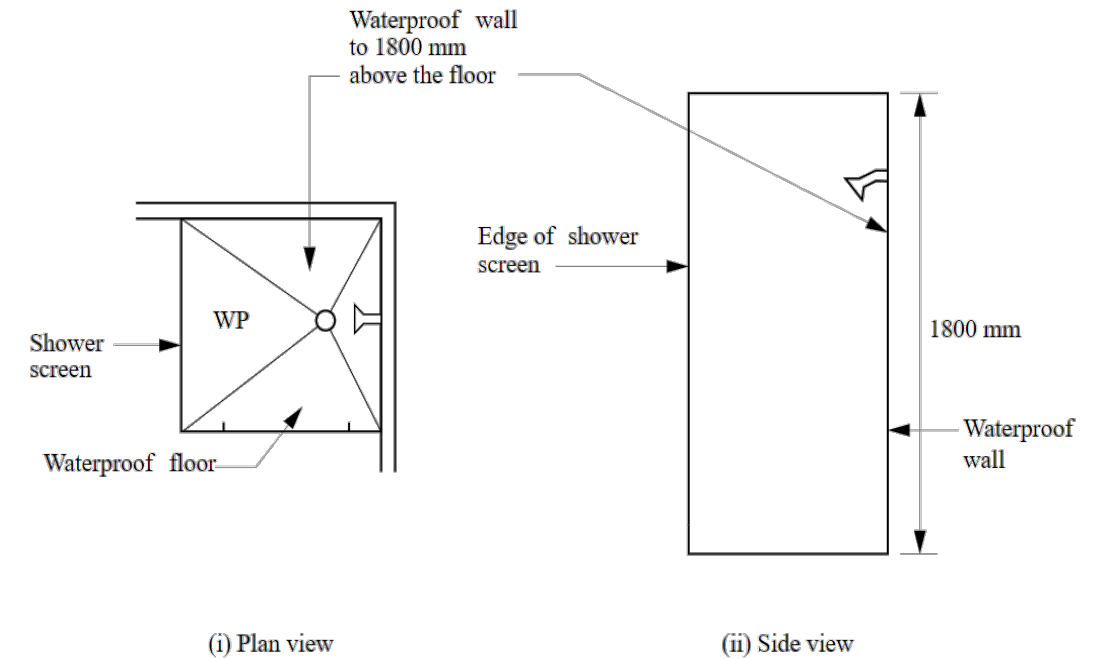

(a) Enclosed shower

Typical detail of enclosed shower as per BCA ABCB Housing Provisions Part 10.2.2

10.2.12 Construction of wet area floors — falls


Where a floor waste is installed—

- (a) the minimum continuous fall of a floor plane to the waste must be 1:80; and
- (b) the maximum continuous fall of a floor plane to the waste must be 1:50.

Floor Waste

app.buildingtools.co

tools

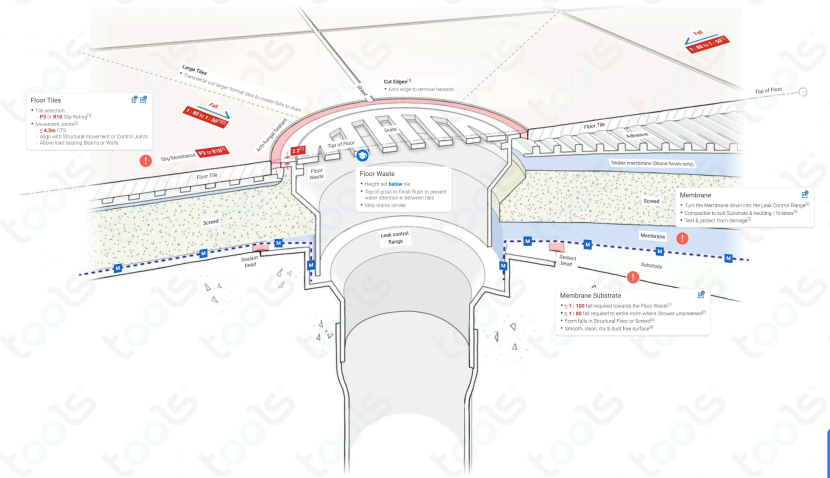

NOTE
The Builder shall check all dimensions and levels on site prior to construction. Notify any errors, discrepancies or omissions to the building designer. Refer to written dimensions only. Do not scale drawings. Drawings shall not be used for construction purposes until issued for construction. This drawing reflects a design by Innovative Eco Designs and is to be used only for work when authorised in writing by Innovative Eco Designs.
All boundaries and contours are subject to survey drawing. All levels to Australian Height Data. It is the contractors responsibility to confirm all measurements on site and locations of any services prior to work on site.
All documents here within are subject to Australian Copyright Laws.



37604191460 ABN
(02) 8710 3852
SUITE 7, 4-10 SELEMS PDE
REVESBY, NSW, 2212
design@iedesigns.com.au
www.iedesigns.com.au



A	01-07-2026	Issue for CDC

DRAWING : **Building Specification**
CLIENT : **Sandstone Constructions**
PROJECT : **PROPOSED SINGLE STOREY DWELLING**
#12, Summer Street, Austral
Lot-2 D.P 1283987

DRAWN BY: **N.B**
SCALE: **1:50**
PAGE SIZE **A3**
DATE : **01-07-2026**
APPLICATION : **CDC**
PAGE NO: **3**
PROJECT NO. **2605 910**
ISSUE **A**

DPC FOR BRICKS

DAMP-PROOF COURSE (DPC) TO EXTENDS THROUGH THE ENTIRE MASONRY LEAF AND NEED TO BE VISIBLE AT THE FINISHED FACE OF THE WALL FROM OUTSIDE



Paragon Building Certifiers Pty Ltd


RBC00045

Registered Certifier

APPROVED


Reference: 260335/01

Date: 16/07/2026

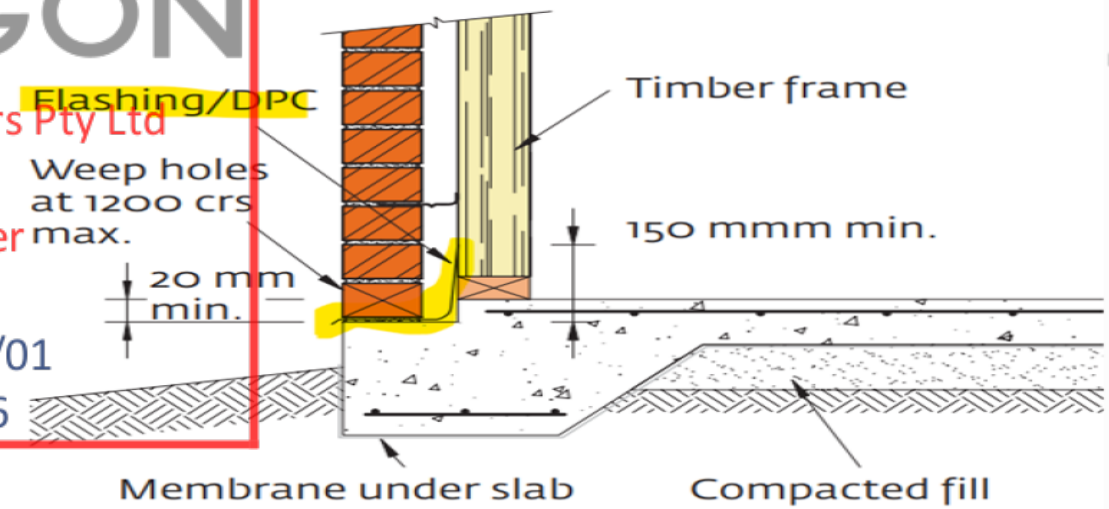

TERMITE SHEET



- TERMITE SHEET EXTENDS THROUGH THE ENTIRE MASONRY LEAF AND IS VISIBLE AT THE FINISHED FACE OF THE WALL.

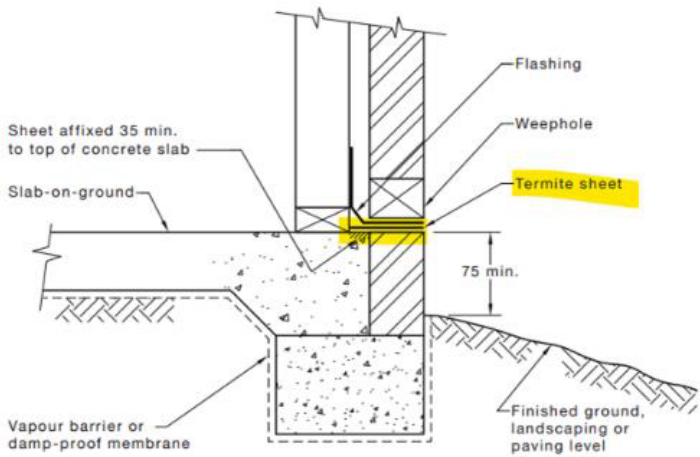

(a) Masonry veneer with separate strip footings

DIMENSIONS IN MILLIMETRES

FIGURE 5.5 (in part) TYPICAL SHEET INSTALLATION TO EXTERNAL WALL WITH CONCRETE FLOOR SLAB

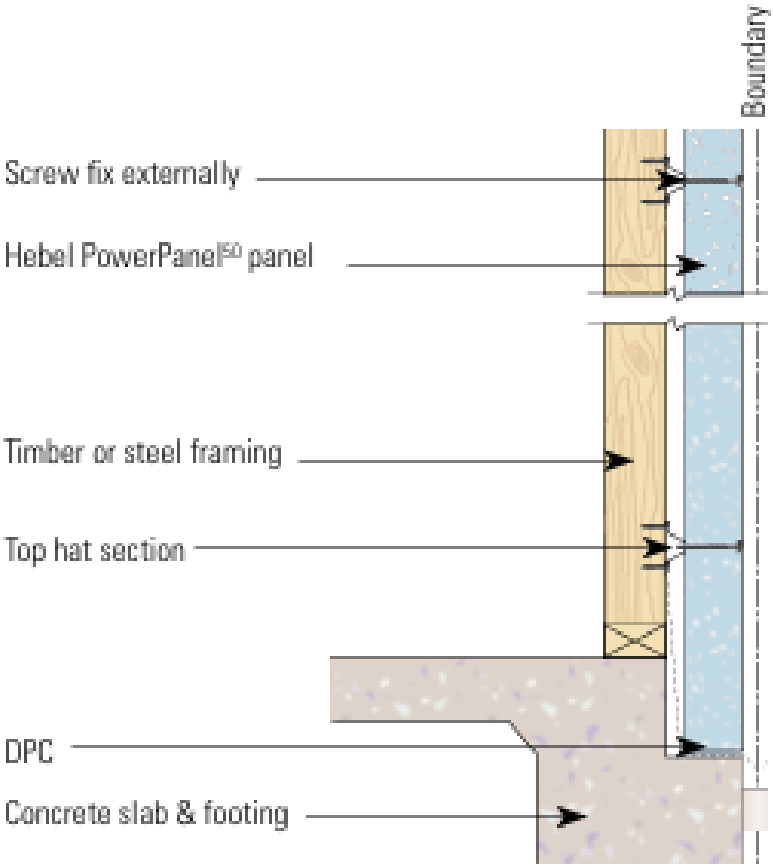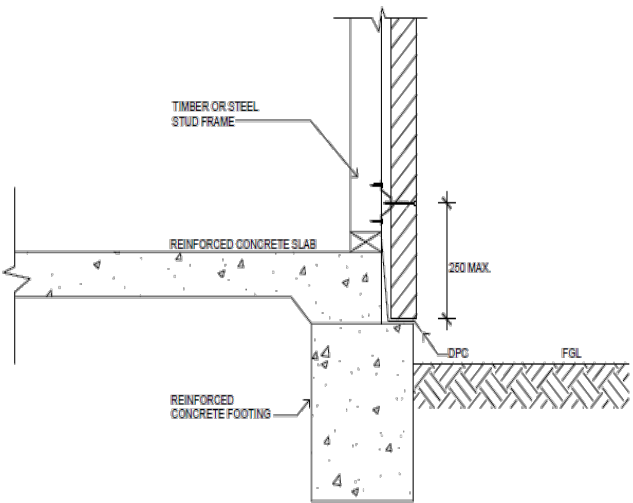

Zero Damage - Zero Harm

NOTE
The Builder shall check all dimensions and levels on site prior to construction. Notify any errors, discrepancies or omissions to the building designer. Refer to written dimensions only. Do not scale drawings. Drawings shall not be used for construction purposes until issued for construction. This drawing reflects a design by Innovative Eco Designs and is to be used only for work when authorised in writing by Innovative Eco Designs.

All boundaries and contours are subject to survey drawing. All levels to Australian Height Data. It is the contractors responsibility to confirm all measurements on site and locations of any services prior to work on site.

All documents here within are subject to Australian Copyright Laws.



37604191460 ABN
(02) 8710 3852
SUITE 7, 4-10 SELEMS PDE
REVESBY, NSW, 2212
design@iedesigns.com.au
www.iedesigns.com.au



A	01-07-2026	Issue for CDC

DRAWING : **Building Specification**
CLIENT : **Sandstone Constructions**
PROJECT : **PROPOSED SINGLE STOREY DWELLING**
#12, Summer Street, Austral
Lot-2 D.P 1283987

DRAWN BY: N.B
SCALE:
PAGE SIZE A3
DATE : **01-07-2026**
APPLICATION : CDC
PAGE NO: 4

PROJECT NO. **2605 910**
ISSUE **A**

Single Dwelling

Certificate number: 1854171S

This certificate confirms that the proposed development will meet the NSW government's requirements for sustainability, if it is built in accordance with the commitments set out below. Terms used in this certificate, or in the commitments, have the meaning given by the document entitled "BASIX Definitions" dated 10/09/2020 published by the Department. This document is available at www.planningportal.nsw.gov.au/definitions

Secretary
Date of issue: Wednesday, 01 July 2026
To be valid, this certificate must be submitted with a development application or lodged with a complying development certificate application within 3 months of the date of issue.

 **Paragon Building Certifiers Pty Ltd**
RBC00045
Registered Certifier
APPROVED
Reference: 260335/01
Date: 16/07/2026

Basix-Commitments
/for details: See the Basix certificate/

- Alternative water**
The applicant must install a rainwater tank of at least 2000 litres.
The rainwater tank to collect rain runoff from at least 130 m2 of the roof
The applicant must connect the rainwater tank to:
- all toilets in the development
 - the cold water tap that supplies each clothes washer
 - at least one outdoor tap in the development

- Fixtures**
- Shower heads 4 star (>6.0 but <= 7.5 L/min)
 - Toilets.....4 star
 - Kitchen tap.....3 star
 - Basin Taps.....3 star

Hot Water System: gas instantaneous with a performance of 6.0 stars /or a system with a higher energy rating

Heating/Cooling: In at least 1 living area and 1 bedroom: 1-phase Air-conditioning; Energy rating: EER - 3.0 (Zoned)

- Ventilation**
- At least 1 Bathroom: individual fan, ducted to façade or roof; Operation control: manual switch on/off
 - Kitchen: individual fan, ducted to façade or roof; Operation control: manual switch on/off
 - Laundry: individual fan, ducted to façade or roof; Operation control: n/a

- Natural lighting**
- The applicant must install a window and/or skylight in the kitchen of the dwelling for natural lighting.
 - The applicant must install a window and/or skylight in 1 bathroom(s)/toilet(s) in the development for natural lighting.

- Artificial lighting fluorescent or (LED)/DEDICATED/:**
- The applicant must ensure that a minimum of 80% of light fixtures are fitted with florescent, compact fluorescent, or light-emitting-diode(LED) lamps.

- OTHER**
- The applicant must install a gas cook top & electric oven in the kitchen of the dwelling.
 - The applicant must install a fixed outdoor clothes drying line as part of the development.



Cut and Fill is only under Slab.
Cut and Fill on the site is minimal, Hence does not
required Retaining wall.

PARAGON

Paragon Building Certifiers Pty Ltd


RBC00045

Registered Certifier

APPROVED

Reference: 260335/01

Date: 16/07/2026

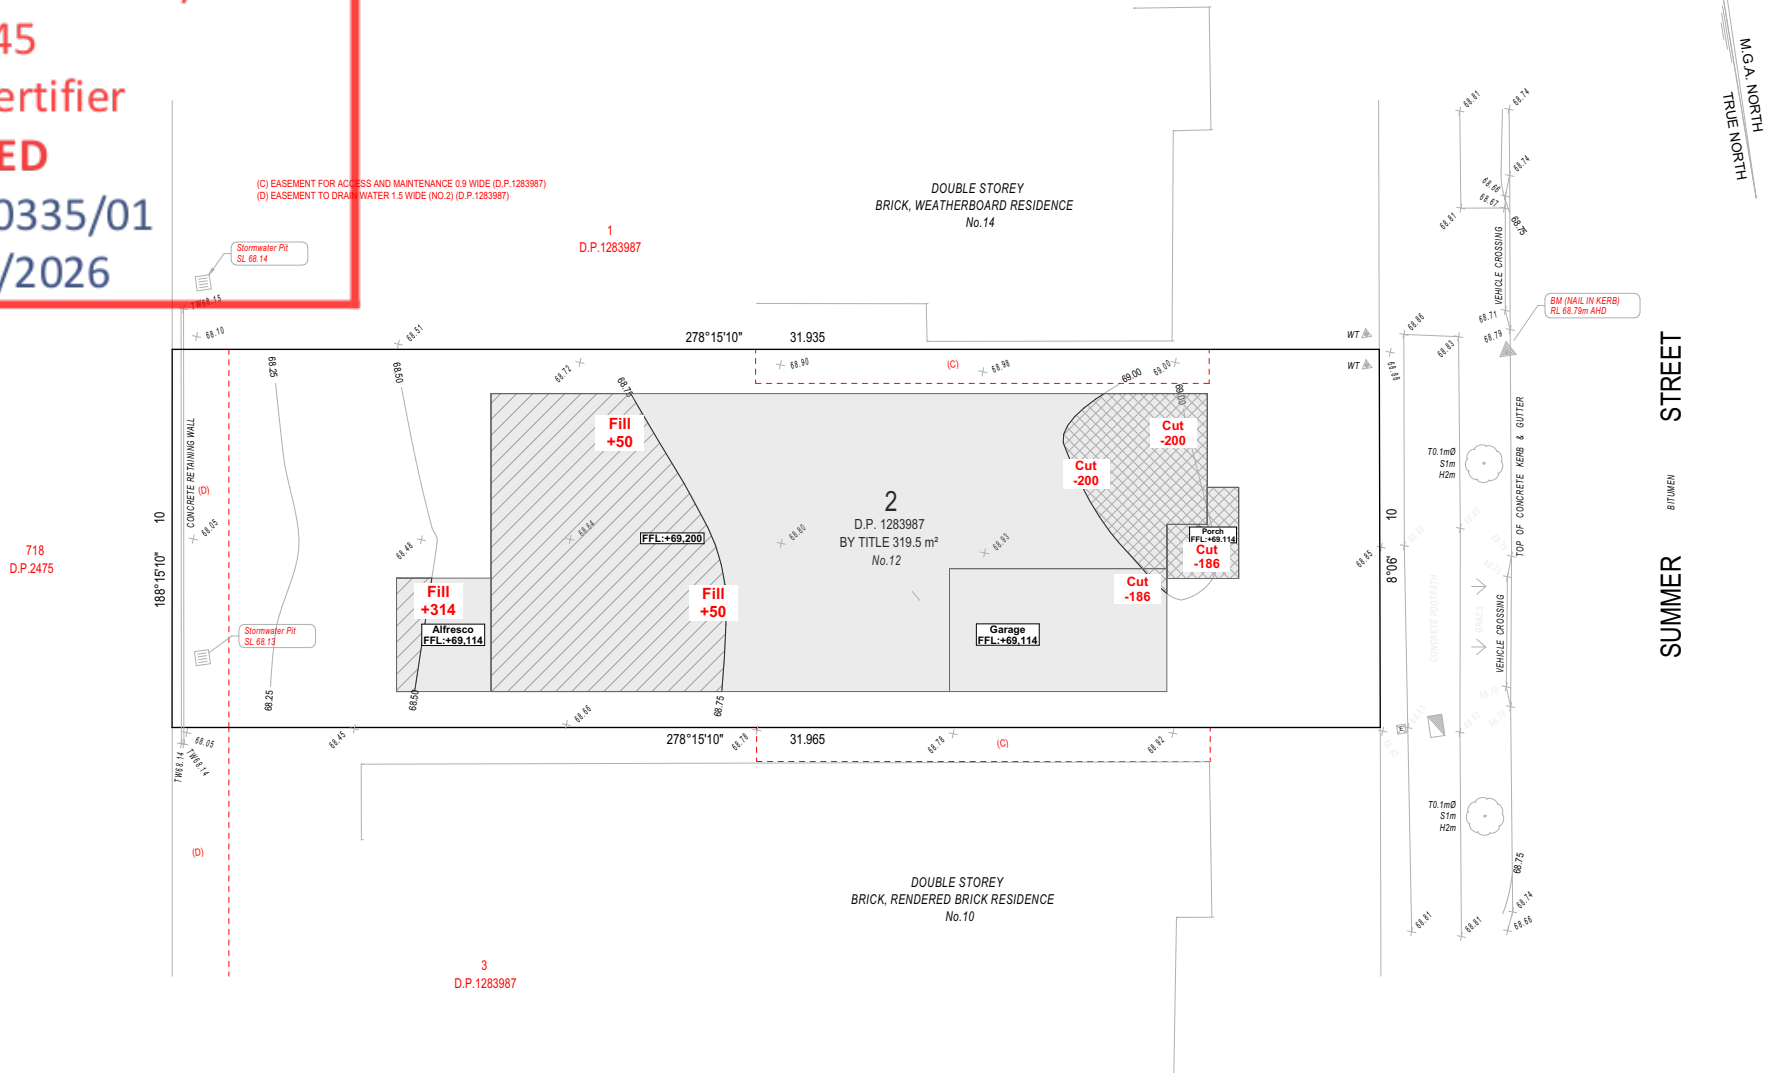

Cut and Fill Plan
1:200



NOTE
The Builder shall check all dimensions and levels on site prior to construction. Notify any errors, discrepancies or omissions to the building designer. Refer to written dimensions only. Do not scale drawings. Drawings shall not be used for construction purposes until issued for construction. This drawing reflects a design by Innovative Eco Designs and is to be used only for work when authorised in writing by Innovative Eco Designs.
All boundaries and contours are subject to survey drawing. All levels to Australian Height Data. It is the contractors responsibility to confirm all measurements on site and locations of any services prior to work on site.
All documents here within are subject to Australian Copyright Laws.



37604191460 ABN
(02) 8710 3852
SUITE 7, 4-10 SELEMS PDE
REVESBY, NSW, 2212
design@iedesigns.com.au
www.iedesigns.com.au



A	01-07-2026	Issue for CDC

DRAWING : **Cut and Fill Plan**
CLIENT : **Sandstone Constructions**
PROJECT : **PROPOSED SINGLE STOREY DWELLING**
#12, Summer Street, Austral
Lot-2 D.P 1283987

DRAWN BY: N.B
SCALE: 1:200
PAGE SIZE A3
DATE : **01-07-2026**
APPLICATION : CDC
PAGE NO: 6

PROJECT NO. **2605 910**
ISSUE **A**

NOTE

- CONCRETE SLAB AS PER ENGINEERS DETAILS
- CONCRETE FOOTINGS AS PER ENGINEER'S DETAILS
- EDGE BEAM DETAILS AS PER ENGINEER'S DETAILS
- ALL BRICK REBATES AS PER ENGINEER'S DETAILS

PARAGON

Paragon Building Certifiers Pty Ltd


RBC00045

Registered Certifier

APPROVED

Reference: 260335/01

Date: 16/07/2026

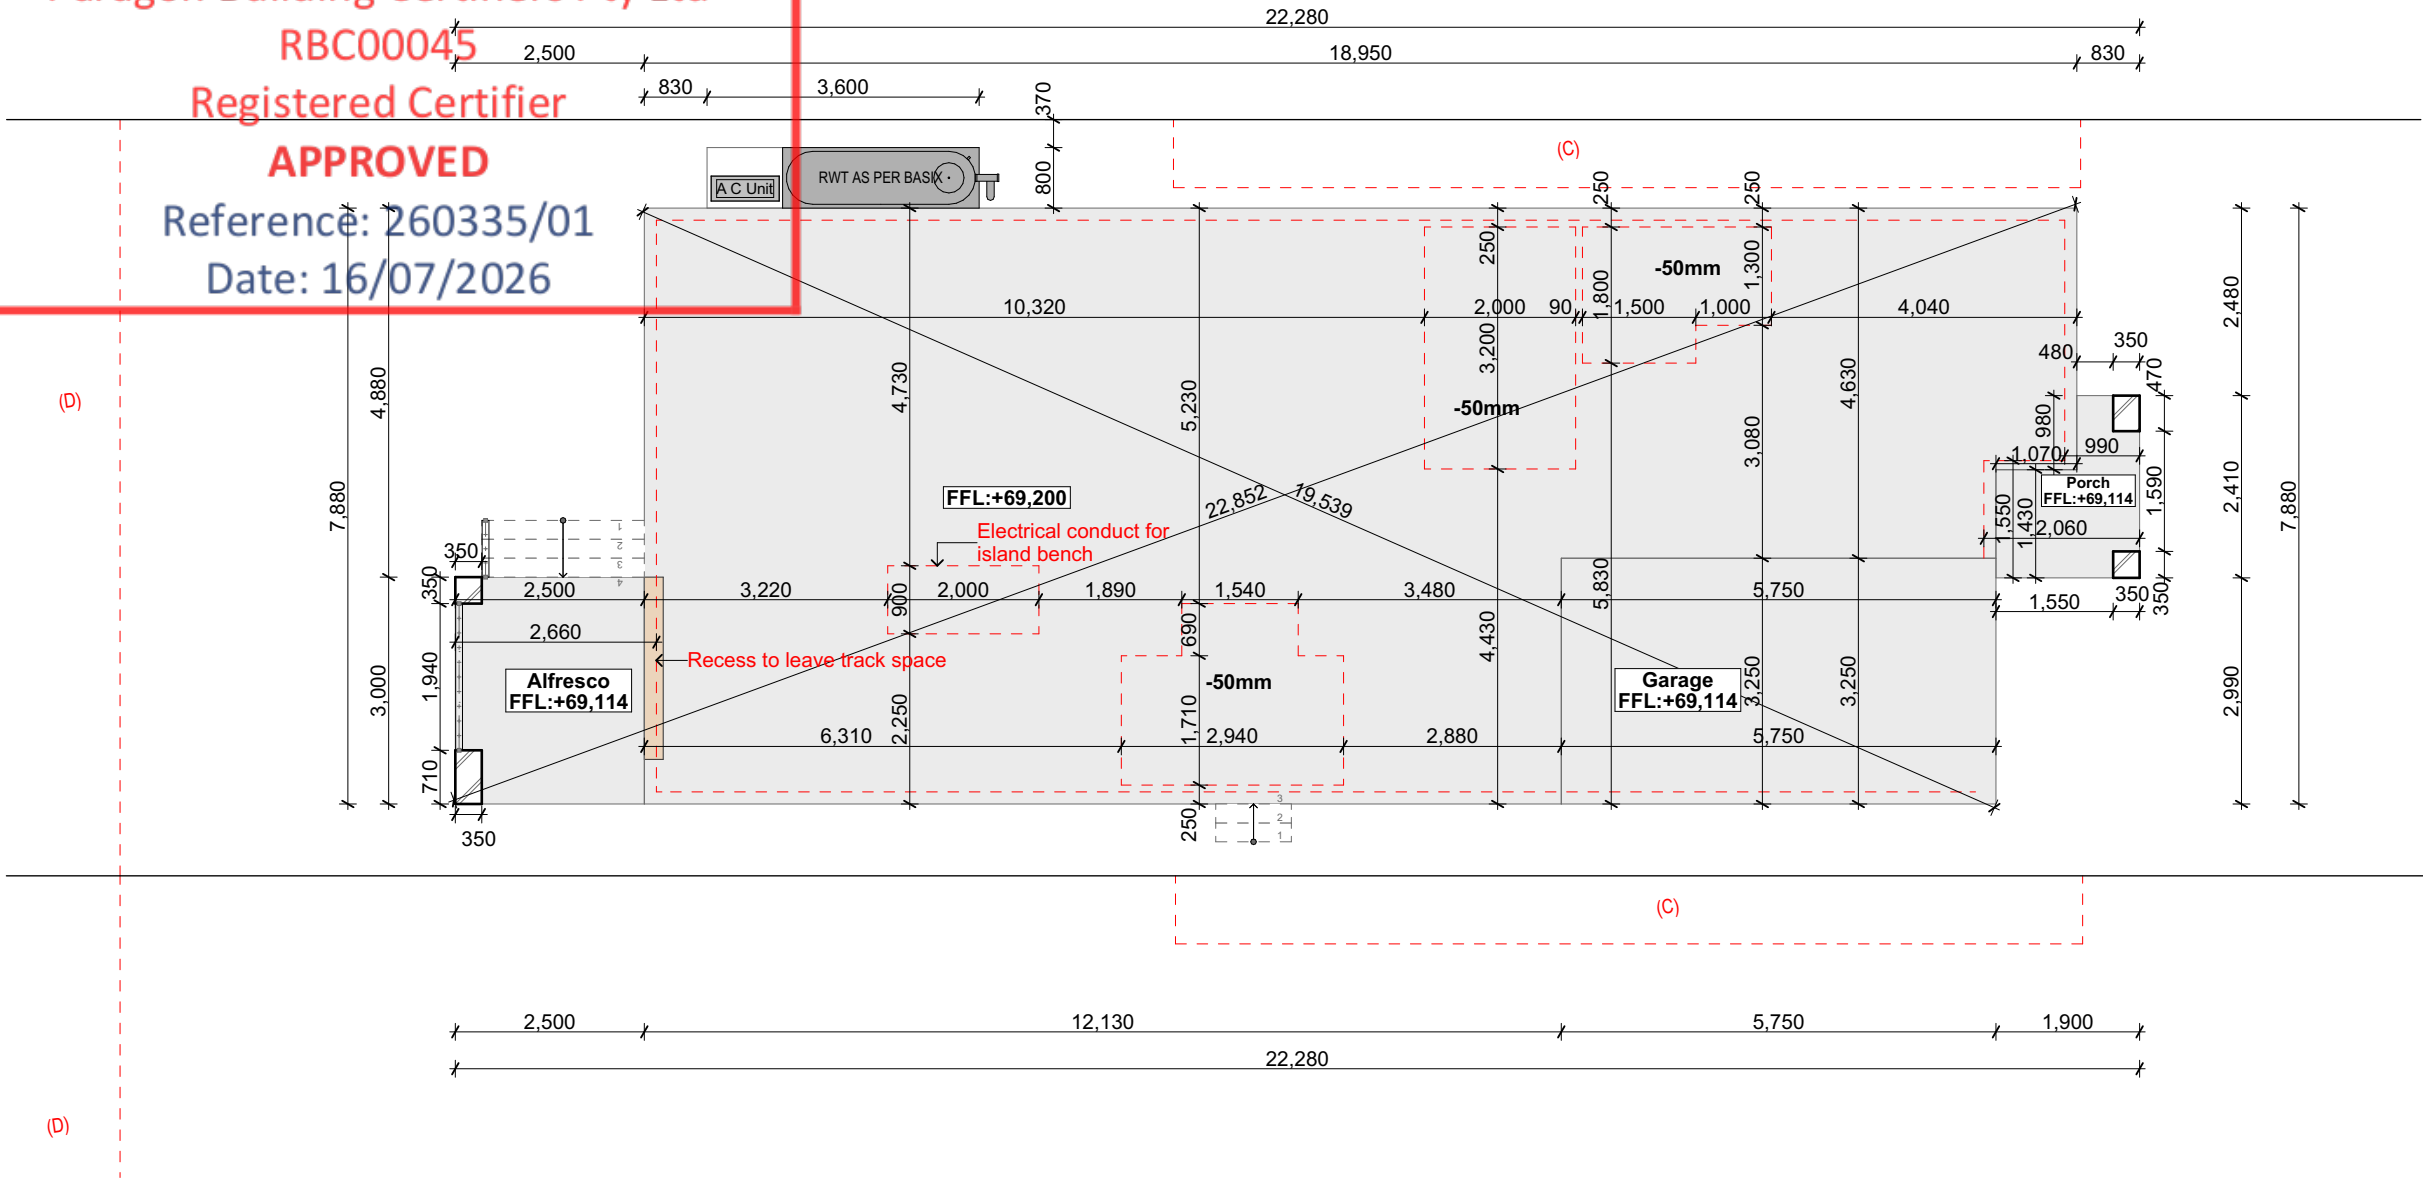

Slab Plan
1:100



NOTE
The Builder shall check all dimensions and levels on site prior to construction. Notify any errors, discrepancies or omissions to the building designer. Refer to written dimensions only. Do not scale drawings. Drawings shall not be used for construction purposes until issued for construction. This drawing reflects a design by Innovative Eco Designs and is to be used only for work when authorised in writing by Innovative Eco Designs.

All boundaries and contours are subject to survey drawing. All levels to Australian Height Data. It is the contractors responsibility to confirm all measurements on site and locations of any services prior to work on site.


All documents here within are subject to Australian Copyright Laws.



37604191460 ABN
(02) 8710 3852
SUITE 7, 4-10 SELEMS PDE
REVESBY, NSW, 2212
design@iedesigns.com.au
www.iedesigns.com.au



A	01-07-2026	Issue for CDC

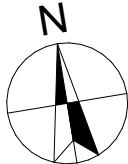

DRAWING : Slab Plan
CLIENT : Sandstone Constructions
PROJECT : PROPOSED SINGLE STOREY DWELLING
#12, Summer Street, Austral
Lot-2 D.P 1283987


DRAWN BY: N.B
SCALE: 1:100
PAGE SIZE A3
DATE : 01-07-2026
APPLICATION : CDC
PAGE NO: 7

PROJECT NO. 2605 910
ISSUE A

of the building line	25.53	8	
of the building line	72.88	23	
	1.85	—	



Paragon Building Certifiers Pty Ltd
RBC00045
Registered Certifier
APPROVED
 Reference: 260335/01
 Date: 16/07/2026

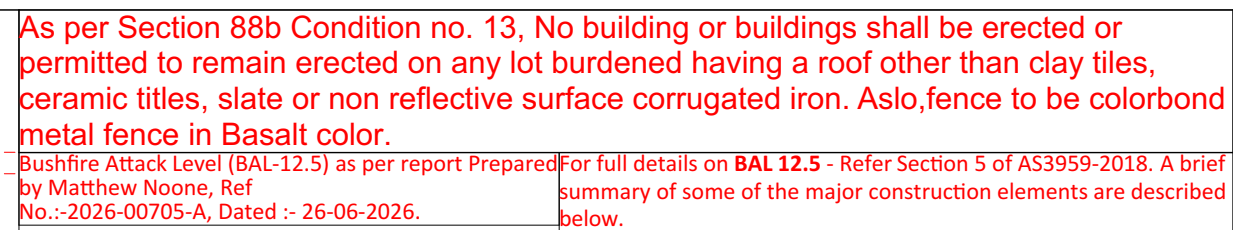

- Floor no special requirements
- Parts less than 400mm above ground or deck etc to be of Non-Combustible Material.
- External Masonry Brick walls
- Fibre cement cladding shall be minimum 6mm thickness
- Vents and weepholes shall be screened. (spark arrestors)
- 4mm Grade A Safety Glass or glass blocks within 400 mm of ground, deck etc with Openable portion metal screened with frame of metal or metal reinforced PVC-U or bushfire resisting timber
- Doors, solid timber minimum thickness 35mm for the first 400 above the threshold. Where doors incorporate glazing it shall be the same as for windows.
- Sliding doors shall be toughened glass 5mm thick minimum. Frames shall be metal or bushfire resistant timber.
- Weather strips shall be provided on garage doors
- Sarking shall comply with Planning for Bushfire Protection 2019 and be placed on top of roof framing.
- Enclosed sub floor decking to be non combustible with in 300mm horizontally and 400mm vertically from framed opening.
- Roof penetrations shall be sealed. All service pipes shall be made of metal.

Note:- this is not an exhaustive list of construction requirements for BAL 12.5. The Builder shall refer to AS3959-2018 and Planning for Bushfire Protection 2019.



<u>SYMBOLS:</u>		<u>SURVEY LEGEND</u>	
BENCHMARK		<u>LEGEND:</u>	
ELECTRICITY BOX		SUBJECT BOUNDARY	
WATER TAP		ADJOINING BOUNDARY	
S/W GRATE		EASEMENT	
TELSTRA PIT		CONTOUR MAJOR	
		CONTOUR MINOR	
		BUILDING LINE	
		TOP KERB	
		WALL	
TREE & TRUNK		<u>LEGEND</u>	
		Ref.img	Mark
			Name
			S.A
			(AS3786 Hard Wired to Mains)
			R.W.T
			Rain Water Tank
			E.M
			Electric Meter
			A/C
			Air Conditioner
			HW
			Wall Mounted
			Hot water System
			P.O.S
			Private Open Space
			FW
			Floor Waste
			MV
			Mechanical Ventilation
			(All vent to exhaust outside).
			ME
			Mechanical Ventilation
			(All vent to exhaust outside).


NOTE

The Builder shall check all dimensions and levels on site prior to construction. Notify any errors, discrepancies or omissions to the building designer. Refer to written dimensions only. Do not scale drawings. Drawings shall not be used for construction purposes until issued for construction. This drawing reflects a design by Innovative Eco Designs and is to be used only for work when authorised in writing by Innovative Eco Designs.

All boundaries and contours are subject to survey drawing. All levels to Australian Height Data. It is the contractors responsibility to confirm all measurements on site and locations of any services prior to work on site.

All documents here within are subject to Australian Copyright Laws.

 INNOVATIVE ECO DESIGNS Your Home Your Style	37604191460 ABN (02) 8710 3852 SUITE 7, 4-10 SELEMS PDE REYESBY, NSW, 2212 design@iedesigns.com.au www.iedesigns.com.au	 BDA A C C R E D I T E D B U I L D I N G D E S I G N E R	<table border="1" style="margin-left: auto; margin-right: auto;"> <tr> <td style="padding: 5px;">A</td> <td style="padding: 5px;">01-07-2026</td> <td style="padding: 5px;">Issue for CDC</td> </tr> </table>	A	01-07-2026	Issue for CDC
A	01-07-2026	Issue for CDC				

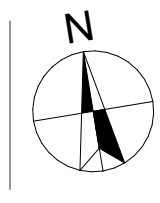

DRAWING : **Site Plan**

CLIENT : **Sandstone Constructions**

PROJECT : **PROPOSED SINGLE STOREY DWELLING**
#12, Summer Street, Austral
Lot-2 D.P 1283987

DRAWN BY: N.B	DATE: 01-07-2026	PROJECT NO. 2605 910
SCALE: 1:200	APPLICATION: CDC	ISSUE A
PAGE SIZE A3	PAGE NO: 8	

2,100

600

1,500

550

NICHE ENTRANCE

400

600

1,200

NICHE IN SHOWER

06

Niche Details

1:50

NICHE ENTRANCE

NICHE IN SHOWER

Niche Details
1:50


- Floor no special requirements
- Parts less than 400mm above ground or deck etc to be of Non-Combustible Material.
- External Masonry Brick walls
- Fibre cement cladding shall be minimum 6mm thickness
- Vents and weepholes shall be screened. (spark arrestors)
- 4mm Grade A Safety Glass or glass blocks within 400 mm of ground, deck etc with Openable portion metal screened with frame of metal or metal reinforced PVC-U or bushfire resisting timber
- Doors, solid timber minimum thickness 35mm for the first 400 above the threshold. Where doors incorporate glazing it shall be the same as for windows.
- Sliding doors shall be toughened glass 5mm thick minimum. Frames shall be metal or bushfire resistant timber.
- Weather strips shall be provided on garage doors
- Sarking shall comply with Planning for Bushfire Protection 2019 and be placed on top of roof framing.
- Enclosed sub floor decking to be non combustible with in 300mm horizontally and 400mm vertically from framed opening.
- Roof penetrations shall be sealed. All service pipes shall be made of metal.

Note:- this is not an exhaustive list of construction requirements for BAL 12.5. The Builder shall refer to AS3959-2018 and Planning for Bushfire Protection 2019.

2,500
Date: 16/07/2026



0. Ground Floor
1:100

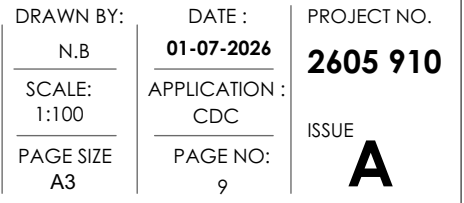

As per Section 88b Condition no. 13, No building or buildings shall be erected or permitted to remain erected on any lot burdened having a roof other than clay tiles, ceramic tiles, slate or non reflective surface corrugated iron. Aslo,fence to be colorbond metal fence in Basalt color.


Bushfire Attack Level (BAL-12.5) as per report Prepared by Matthew Noone, Ref No.:-2026-00705-A, Dated :- 26-06-2026.



For full details on **BAL 12.5** - Refer Section 5 of AS3959-2018. A brief summary of some of the major construction elements are described below.

- Floor no special requirements
- Parts less than 400mm above ground or deck etc to be of Non-Combustible Material.
- External Masonry Brick walls
- Fibre cement cladding shall be minimum 6mm thickness
- Vents and weepholes shall be screened. (spark arrestors)
- 4mm Grade A Safety Glass or glass blocks within 400 mm ofground, deck etc with Openable portion metal screened withframe of metal or metal reinforced PVC-U or bushfire resisting timber
- Doors, solid timber minimum thickness 35mm for the first 400 above the threshold. Where doors incorporate glazing it shall be the same as for windows.
- Sliding doors shall be toughened glass 5mm thick minimum. Frames shall be metal or bushfire resistant timber.
- Weather strips shall be provided on garage doors
- Sarking shall comply with Planning for Bushfire Protection 2019 and be placed on top of roof framing.
- Enclosed sub floor decking to be non combustible with in 300mm horizontally and 400mm vertically from framed opening.
- Roof penetrations shall be sealed. All service pipes shall be made of metal.

Note:- this is not an exhaustive list of construction requirements for BAL 12.5. The Builder shall refer to AS3959-2018 and Planning for Bushfire Protection 2019.

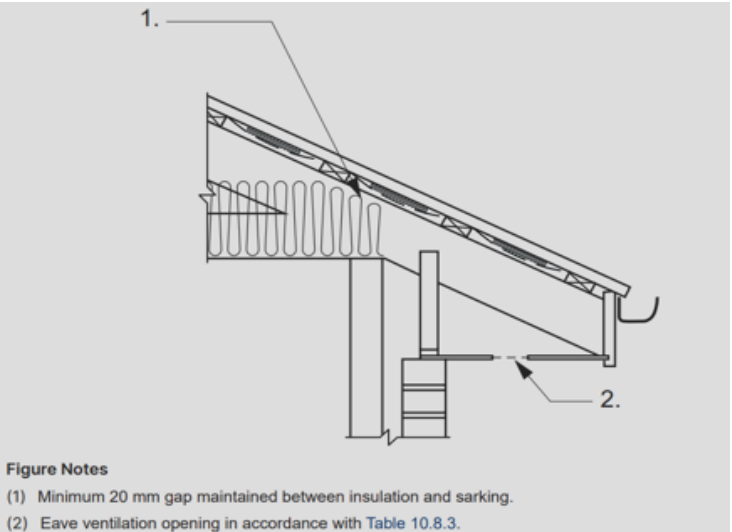

VENTILATION OF ROOF SPACES



ROOF SPACE AS PER 10.8.3 1(a) & 1(b)

- (i) VENTILATED TO OUTDOOR AIR THROUGH EVENLY DISTRIBUTED OPENINGS IN ACCORDANCE WITH TABLE 10.8.3; OR
- (ii) LOCATED IMMEDIATELY UNDERNEATH THE ROOF TILES OF AN UNSARKED TILED ROOF.

TABLE 10.8.3: ROOF SPACE VENTILATION REQUIREMENTS

ROOF PITCH	VENTILATION OPENINGS
$\geq 15^\circ$ AND $< 75^\circ$	7,000 MM ² /M PROVIDED AT THE EAVES AND 5,000 MM ² /M AT HIGH LEVEL, PLUS AN ADDITIONAL 18,000 MM ² /M AT THE EAVES IF THE ROOF HAS A CATHEDRAL CEILING

Figure 7.2.3: Minimum pitch requirements for metal roofing profiles

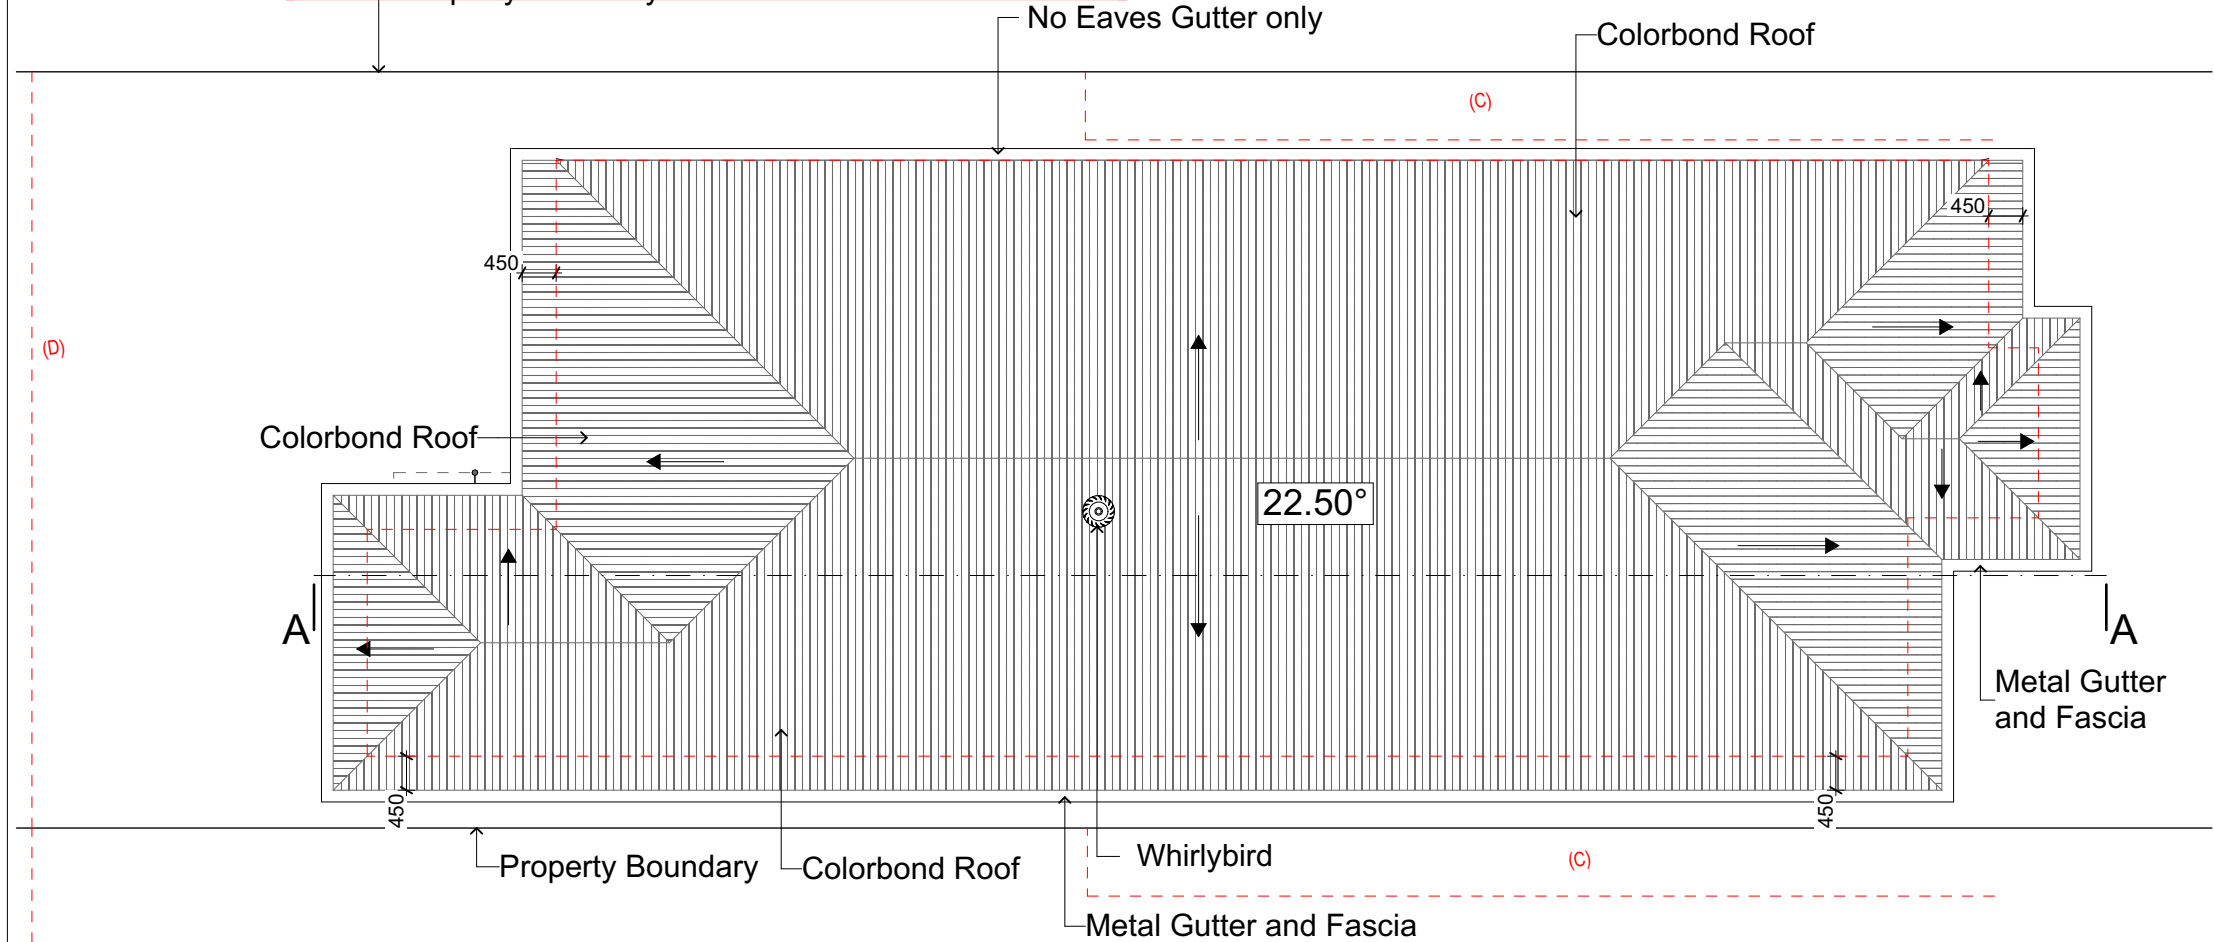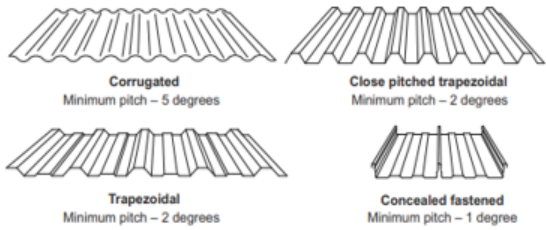

Roof
1:100

NOTE
The Builder shall check all dimensions and levels on site prior to construction. Notify any errors, discrepancies or omissions to the building designer. Refer to written dimensions only. Do not scale drawings. Drawings shall not be used for construction purposes until issued for construction. This drawing reflects a design by Innovative Eco Designs and is to be used only for work when authorised in writing by Innovative Eco Designs.

All boundaries and contours are subject to survey drawing. All levels to Australian Height Data. It is the contractors responsibility to confirm all measurements on site and locations of any services prior to work on site.


All documents here within are subject to Australian Copyright Laws.



37604191460 ABN
(02) 8710 3852
SUITE 7, 4-10 SELEMS PDE
REVESBY, NSW, 2212
design@iedesigns.com.au
www.iedesigns.com.au




A	01-07-2026	Issue for CDC

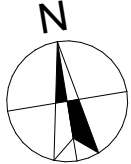

DRAWING : **Roof Plan**
CLIENT : **Sandstone Constructions**
PROJECT : **PROPOSED SINGLE STOREY DWELLING**
#12,Summer Street,Austral
Lot-2 D.P 1283987

DRAWN BY: N.B
SCALE: 1:100
PAGE SIZE A3
DATE : **01-07-2026**
APPLICATION : CDC
PAGE NO: 10

PROJECT NO. **2605 910**
ISSUE **A**

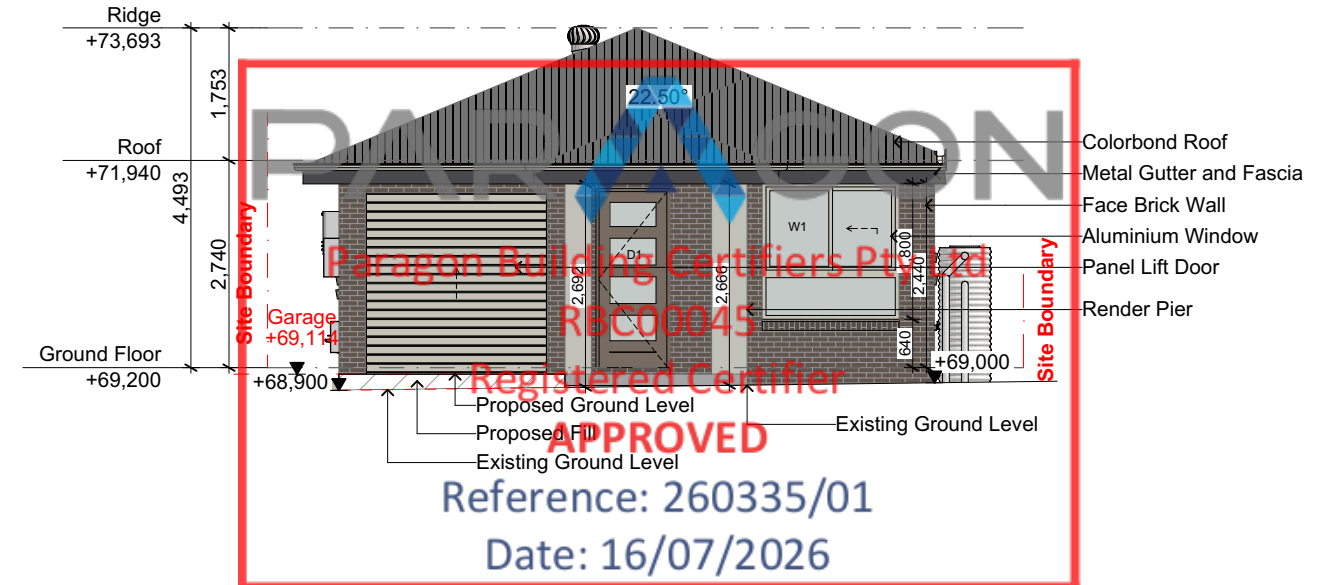

1 East Elevation (Front)
1:100

Ground floor windows to touch the eaves.

As per Section 88b Condition no. 13, No building or buildings shall be erected or permitted to remain erected on any lot burdened having a roof other than clay tiles, ceramic tiles, slate or non reflective surface corrugated iron. Aslo,fence to be colorbond metal fence in Basalt color.

Bushfire Attack Level (BAL-12.5) as per report Prepared by Matthew Noone, Ref No.:-2026-00705-A, Dated :- 26-06-2026.

For full details on **BAL 12.5** - Refer Section 5 of AS3959-2018. A brief summary of some of the major construction elements are described below.

- Floor no special requirements
- Parts less than 400mm above ground or deck etc to be of Non-Combustible Material.
- External Masonry Brick walls
- Fibre cement cladding shall be minimum 6mm thickness
- Vents and weepholes shall be screened. (spark arrestors)
- 4mm Grade A Safety Glass or glass blocks within 400 mm ofground, deck etc with Openable portion metal screened withframe of metal or metal reinforced PVC-U or bushfire resisting timber
- Doors, solid timber minimum thickness 35mm for the first 400 above the threshold. Where doors incorporate glazing it shall be the same as for windows.
- Sliding doors shall be toughened glass 5mm thick minimum. Frames shall be metal or bushfire resistant timber.
- Weather strips shall be provided on garage doors
- Sarking shall comply with Planning for Bushfire Protection 2019 and be placed on top of roof framing.
- Enclosed sub floor decking to be non combustible with in 300mm horizontally and 400mm vertically from framed opening.
- Roof penetrations shall be sealed. All service pipes shall be made of metal.

Note:- this is not an exhaustive list of construction requirements for BAL 12.5. The Builder shall refer to AS3959-2018 and Planning for Bushfire Protection 2019.



2 West Elevation (Rear)
1:100



NOTE
The Builder shall check all dimensions and levels on site prior to construction. Notify any errors, discrepancies or omissions to the building designer. Refer to written dimensions only. Do not scale drawings. Drawings shall not be used for construction purposes until issued for construction. This drawing reflects a design by Innovative Eco Designs and is to be used only for work when authorised in writing by Innovative Eco Designs.
All boundaries and contours are subject to survey drawing. All levels to Australian Height Data. It is the contractors responsibility to confirm all measurements on site and locations of any services prior to work on site.
All documents here within are subject to Australian Copyright Laws.



37604191460 ABN
(02) 8710 3852
SUITE 7, 4-10 SELEMS PDE
REVESBY, NSW, 2212
design@iedesigns.com.au
www.iedesigns.com.au



A	01-07-2026	Issue for CDC

DRAWING : **Elevation**
CLIENT : **Sandstone Constructions**
PROJECT : **PROPOSED SINGLE STOREY DWELLING**
#12,Summer Street,Austral
Lot-2 D.P 1283987

DRAWN BY: N.B	DATE : 01-07-2026	PROJECT NO. 2605 910
SCALE: 1:100	APPLICATION : CDC	ISSUE A
PAGE SIZE A3	PAGE NO: 11	


Ground floor windows to touch the eaves.

As per Section 88b Condition no. 13, No building or buildings shall be erected or permitted to remain erected on any lot burdened having a roof other than clay tiles, ceramic tiles, slate or non reflective surface corrugated iron. Aslo,fence to be colorbond metal fence in Basalt color.

Bushfire Attack Level (BAL-12.5) as per report Prepared by Matthew Noone, Ref No.:-2026-00705-A, Dated :- 26-06-2026.
For full details on **BAL 12.5** - Refer Section 5 of AS3959-2018. A brief summary of some of the major construction elements are described below.

- Floor no special requirements
- Parts less than 400mm above ground or deck etc to be of Non-Combustible Material.
- External Masonry Brick walls
- Fibre cement cladding shall be minimum 6mm thickness
- Vents and weepholes shall be screened. (spark arrestors)
- 4mm Grade A Safety Glass or glass blocks within 400 mm ofground, deck etc with Openable portion metal screened withframe of metal or metal reinforced PVC-U or bushfire resisting timber
- Doors, solid timber minimum thickness 35mm for the first 400 above the threshold. Where doors incorporate glazing it shall be the same as for windows.
- Sliding doors shall be toughened glass 5mm thick minimum. Frames shall be metal or bushfire resistant timber.
- Weather strips shall be provided on garage doors
- Sarking shall comply with Planning for Bushfire Protection 2019 and be placed on top of roof framing.
- Enclosed sub floor decking to be non combustible with in 300mm horizontally and 400mm vertically from framed opening.
- Roof penetrations shall be sealed. All service pipes shall be made of metal.

Note:- this is not an exhaustive list of construction requirements for BAL 12.5. The Builder shall refer to AS3959-2018 and Planning for Bushfire Protection 2019.

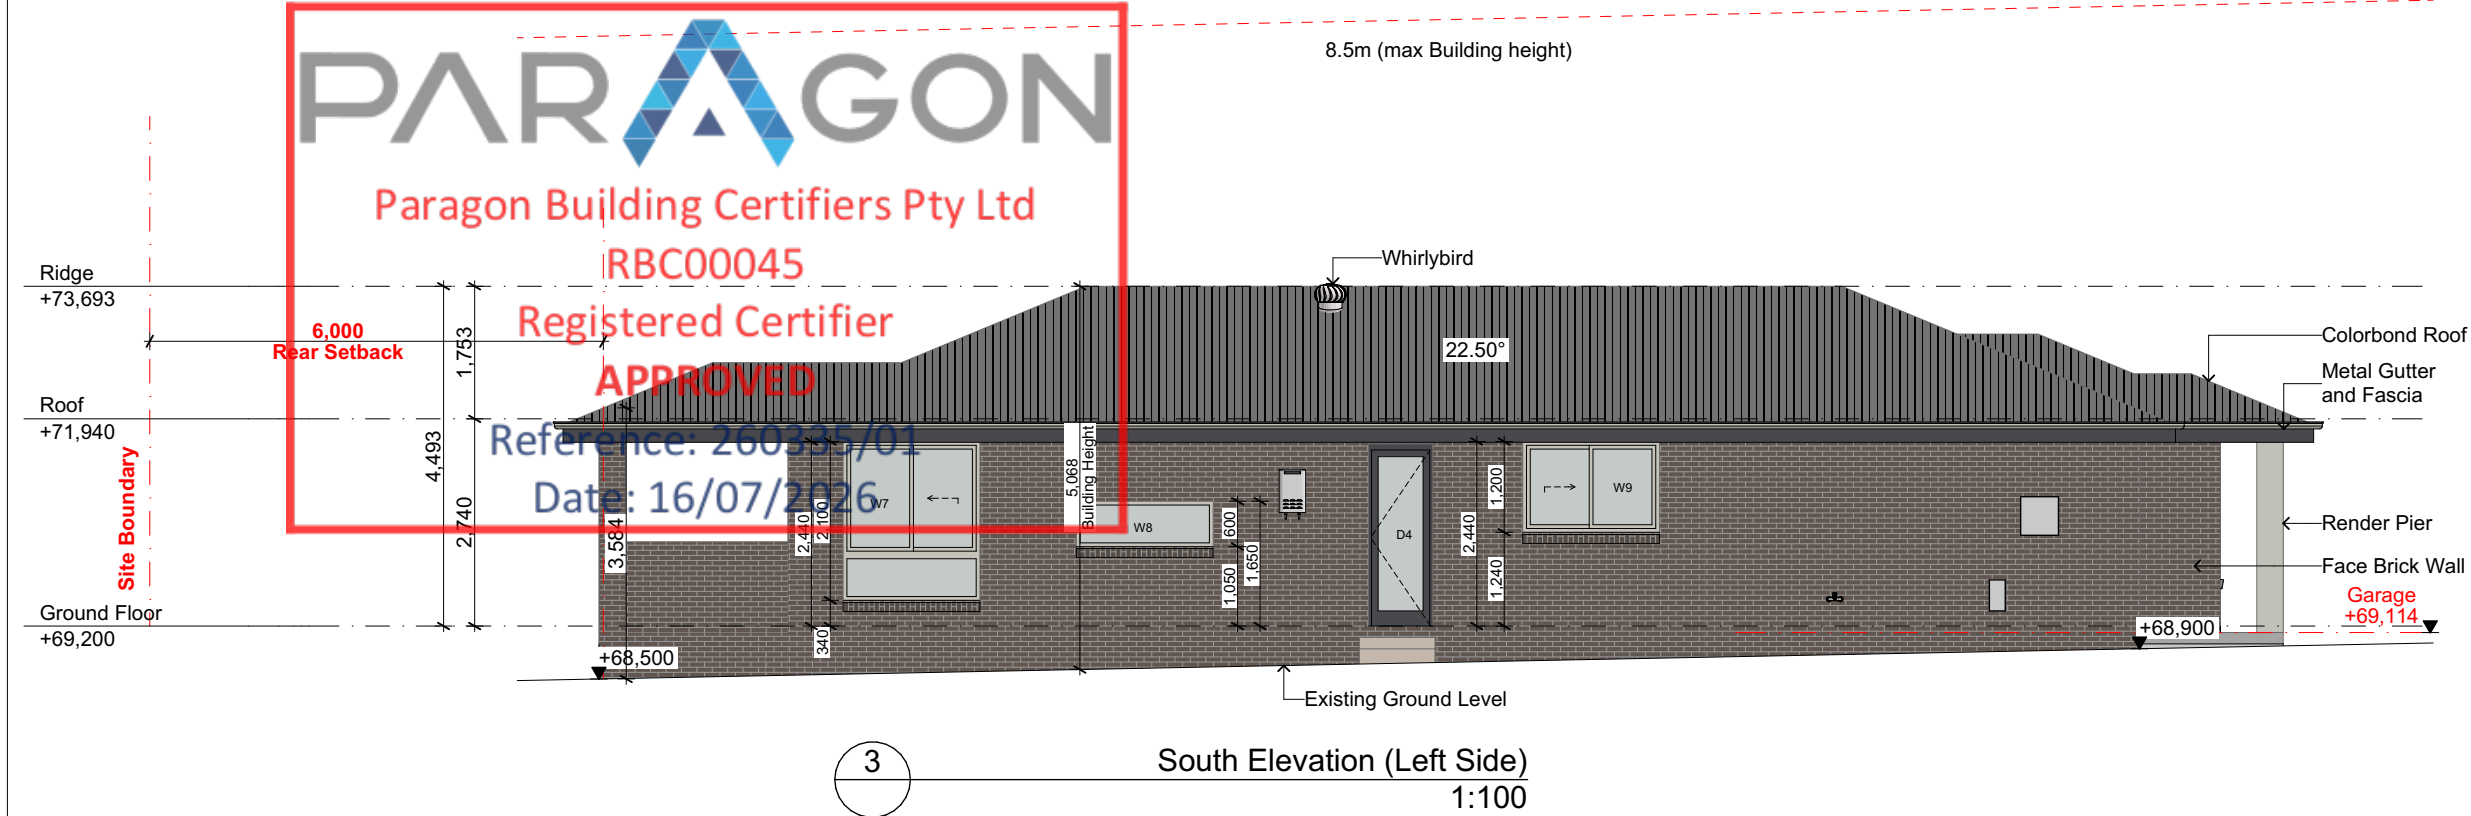

NOTE
The Builder shall check all dimensions and levels on site prior to construction. Notify any errors, discrepancies or omissions to the building designer. Refer to written dimensions only. Do not scale drawings. Drawings shall not be used for construction purposes until issued for construction. This drawing reflects a design by Innovative Eco Designs and is to be used only for work when authorised in writing by Innovative Eco Designs.
All boundaries and contours are subject to survey drawing. All levels to Australian Height Data. It is the contractors responsibility to confirm all measurements on site and locations of any services prior to work on site.
All documents here within are subject to Australian Copyright Laws.



37604191460 ABN
(02) 8710 3852
SUITE 7, 4-10 SELEMS PDE
REVESBY, NSW, 2212
design@iedesigns.com.au
www.iedesigns.com.au



A	01-07-2026	Issue for CDC

DRAWING : **Side Elevation**
CLIENT : **Sandstone Constructions**
PROJECT : **PROPOSED SINGLE STOREY DWELLING**
#12, Summer Street, Austral
Lot-2 D.P 1283987

DRAWN BY:	DATE :	PROJECT NO.
N.B	01-07-2026	2605 910
SCALE:	APPLICATION :	ISSUE
1:100	CDC	A
PAGE SIZE	PAGE NO:	
A3	12	


As per Section 88b Condition no. 13, No building or buildings shall be erected or permitted to remain erected on any lot burdened having a roof other than clay tiles, ceramic tiles, slate or non reflective surface corrugated iron. Aslo,fence to be colorbond metal fence in Basalt color.

Bushfire Attack Level (BAL-12.5) as per report Prepared by Matthew Noone, Ref No.:-2026-00705-A, Dated :- 26-06-2026.

For full details on **BAL 12.5** - Refer Section 5 of AS3959-2018. A brief summary of some of the major construction elements are described below.

- Floor no special requirements
- Parts less than 400mm above ground or deck etc to be of Non-Combustible Material.
- External Masonry Brick walls
- Fibre cement cladding shall be minimum 6mm thickness
- Vents and weepholes shall be screened. (spark arrestors)
- 4mm Grade A Safety Glass or glass blocks within 400 mm ofground, deck etc with Openable portion metal screened withframe of metal or metal reinforced PVC-U or bushfire resisting timber
- Doors, solid timber minimum thickness 35mm for the first 400 above the threshold. Where doors incorporate glazing it shall be the same as for windows.
- Sliding doors shall be toughened glass 5mm thick minimum. Frames shall be metal or bushfire resistant timber.
- Weather strips shall be provided on garage doors
- Sarking shall comply with Planning for Bushfire Protection 2019 and be placed on top of roof framing.
- Enclosed sub floor decking to be non combustible with in 300mm horizontally and 400mm vertically from framed opening.
- Roof penetrations shall be sealed. All service pipes shall be made of metal.

Note:- this is not an exhaustive list of construction requirements for BAL 12.5. The Builder shall refer to AS3959-2018 and Planning for Bushfire Protection 2019.

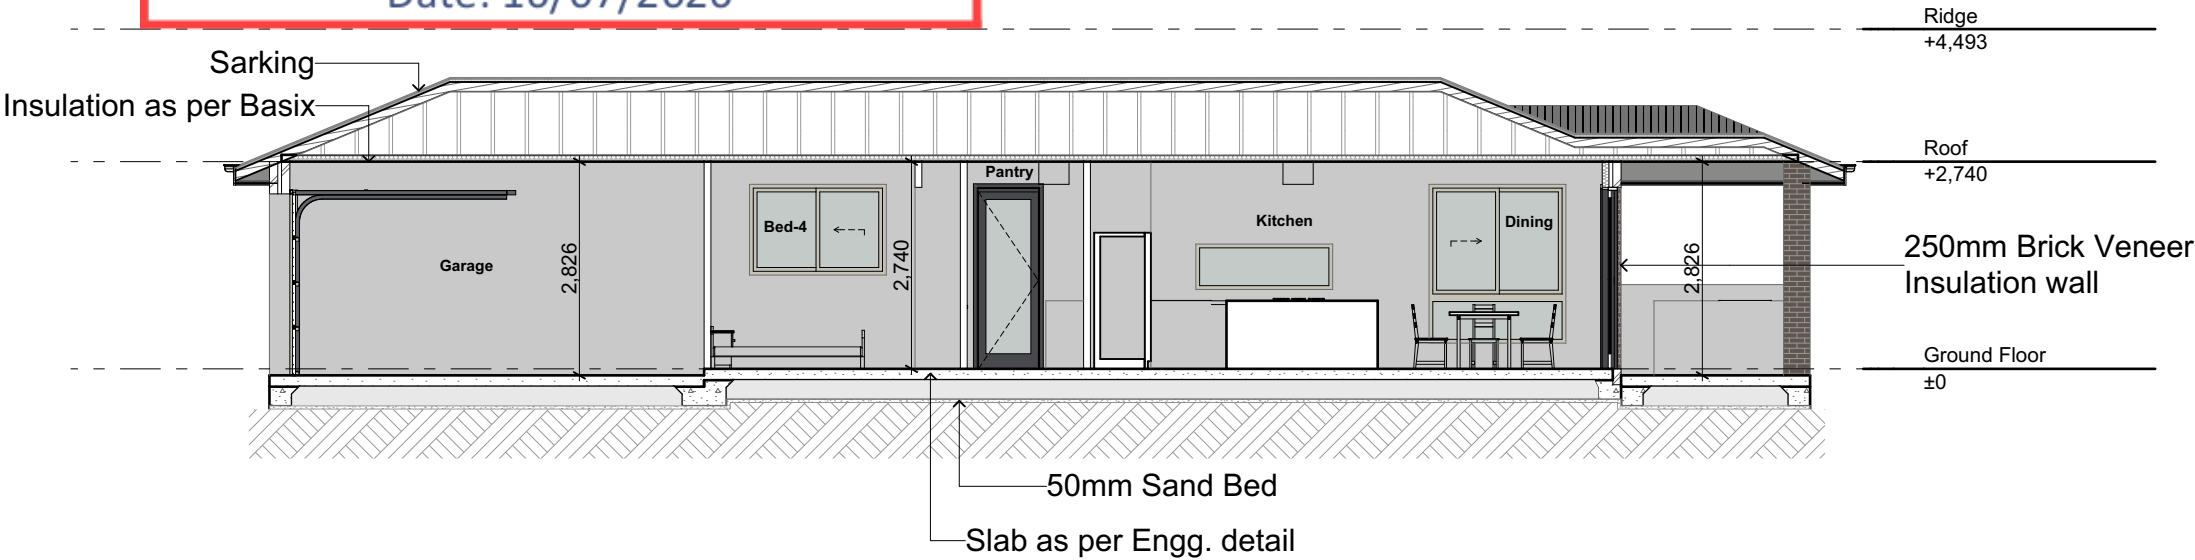

NOTE
The Builder shall check all dimensions and levels on site prior to construction. Notify any errors, discrepancies or omissions to the building designer. Refer to written dimensions only. Do not scale drawings. Drawings shall not be used for construction purposes until issued for construction. This drawing reflects a design by Innovative Eco Designs and is to be used only for work when authorised in writing by Innovative Eco Designs.

All boundaries and contours are subject to survey drawing. All levels to Australian Height Data. It is the contractors responsibility to confirm all measurements on site and locations of any services prior to work on site.

All documents here within are subject to Australian Copyright Laws.



37604191460 ABN
(02) 8710 3852
SUITE 7, 4-10 SELEMS PDE
REVESBY, NSW, 2212
design@iedesigns.com.au
www.iedesigns.com.au



A	01-07-2026	Issue for CDC

DRAWING : **Section**

CLIENT : **Sandstone Constructions**

PROJECT : **PROPOSED SINGLE STOREY DWELLING**
#12, Summer Street, Austral
Lot-2 D.P 1283987

DRAWN BY: N.B

SCALE: 1:100

PAGE SIZE A3

DATE : **01-07-2026**

APPLICATION : CDC

PAGE NO: 13

PROJECT NO. **2605 910**

ISSUE **A**

Door Schedule						
ID	D1	D2	D3	OPEN	OPEN	
Wallhole Dimensions(W x H)	980×2,370	880×2,410	780×2,410	800×2,400	900×2,400	
Leaf Dimensions	920×2,340	820×2,340	720×2,340	---	---	
Elevation						
Total Glazed Area SQM	0.83	0.00	0.00	---	---	0.83
Position	Exterior	Interior	Interior	Interior	Interior	
Quantity	1	5	2	1	1	10
Aluminium Door Schedule						
ID	D4	Panel Lift	SD5			
Frame Dimensions (W X H)	850×2,410	2,410×2,400	2,410×2,400			
Elevation						
Total Glazed Area SQM	1.21	0.60	3.56			5.37
Glazed Area SQM	---	---	---			0.00
Position	Exterior	Exterior	Exterior			
Quantity	1	1	1			3

Bushfire Attack Level (BAL-12.5) as per report Prepared by Matthew Noone, Ref No.:-2026-00705-A, Dated :- 26-06-2026.
For full details on **BAL 12.5** - Refer Section 5 of AS3959-2018. A brief summary of some of the major construction elements are described below.

- Floor no special requirements
- Parts less than 400mm above ground or deck etc to be of Non-Combustible Material.
- External Masonry Brick walls
- Fibre cement cladding shall be minimum 6mm thickness
- Vents and weepholes shall be screened. (spark arrestors)
- 4mm Grade A Safety Glass or glass blocks within 400 mm ofground, deck etc with Openable portion metal screened withframe of metal or metal reinforced PVC-U or bushfire resisting timber
- Doors, solid timber minimum thickness 35mm for the first 400 above the threshold. Where doors incorporate glazing it shall be the same as for windows.
- Sliding doors shall be toughened glass 5mm thick minimum. Frames shall be metal or bushfire resistant timber.
- Weather strips shall be provided on garage doors
- Sarking shall comply with Planning for Bushfire Protection 2019 and be placed on top of roof framing.
- Enclosed sub floor decking to be non combustible with in 300mm horizontally and 400mm vertically from framed opening.
- Roof penetrations shall be sealed. All service pipes shall be made of metal.

Note:- this is not an exhaustive list of construction requirements for BAL 12.5. The Builder shall refer to AS3959-2018 and Planning for Bushfire Protection 2019.

SCHEDULE OF FINISHES		
Element	SPECIFICATION	COLOUR
Walls	Brick-Elevation Ridge	
Render Finish Pier	Surfmist	
Roof	Colorbond-Monument	
Gutter	Surfmist	
Fascia	Monument	
Window	Surfmist	
Garage Door Colour	Surfmist	

As per Section 88b Condition no. 13, No building or buildings shall be erected or permitted to remain erected on any lot burdened having a roof other than clay tiles, ceramic tiles, slate or non reflective surface corrugated iron. Aslo,fence to be colorbond metal fence in Basalt color.



NOTE
The Builder shall check all dimensions and levels on site prior to construction. Notify any errors, discrepancies or omissions to the building designer. Refer to written dimensions only. Do not scale drawings. Drawings shall not be used for construction purposes until issued for construction. This drawing reflects a design by Innovative Eco Designs and is to be used only for work when authorised in writing by Innovative Eco Designs.

All boundaries and contours are subject to survey drawing. All levels to Australian Height Data. It is the contractors responsibility to confirm all measurements on site and locations of any services prior to work on site.

All documents here within are subject to Australian Copyright Laws.










37604191460 **ABN**
(02) 8710 3852
SUITE 7, 4-10 SELEMS PDE
REVESBY, NSW,2212
design@iedesigns.com.au
www.iedesigns.com.au




A	01-07-2026	Issue for CDC

DRAWING : **Door Schedule & SOF**
CLIENT : **Sandstone Constructions**
PROJECT : **PROPOSED SINGLE STOREY DWELLING**
#12,Summer Street,Austral
Lot-2 D.P 1283987

DRAWN BY: N.B	DATE : 01-07-2026	PROJECT NO. 2605 910
SCALE:	APPLICATION : CDC	ISSUE A
PAGE SIZE A3	PAGE NO: 14	

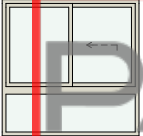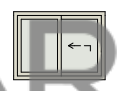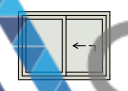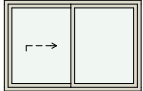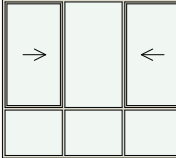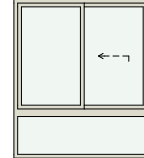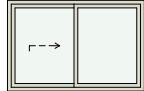Window Schedule										
ID	W1	W2	W3	W4	W5	W6	W7	W8	W9	
Frame Dimensions	1,810×1,800	1,210×900	1,210×900	1,810×1,200	1,810×1,200	2,410×2,100	1,810×2,100	1,810×600	1,810×1,200	
Elevation										
Glass	Glass - Clear	Glass - Obscure	Glass - Obscure	Glass - Clear	Glass - Clear	Glass - Clear	Glass - Clear	Glass - Clear	Glass - Clear	
Glazed Area SQM	2.42	0.67	0.67	1.56	1.56	0.00	2.88	0.86	1.56	12.18
Quantity	1	1	1	1	1	1	1	1	1	9

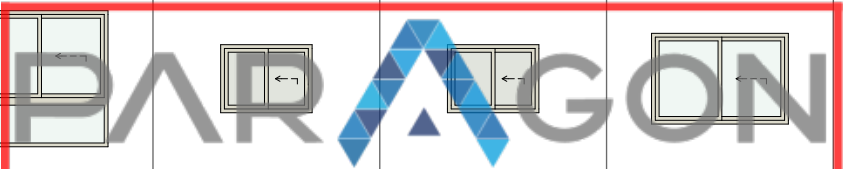

Paragon Building Certifiers Pty Ltd

RBC00045

Registered Certifier

APPROVED

Reference: 260335/01

Date: 16/07/2026

NOTE:
- TO BE CHECKED AND CONFIRMED BY BUILDER ON SITE BEFORE PLACING ORDER.
-FALL PREVENTION FROM WINDOWS
-WINDOWS TO BE MANUFACTURED IN ACCORDANCE WITH REQUIREMENTS OF NCC 2022 vol. 2 part 11.3.7
1- If Opening withing 1700mm above the floor; and climable elements between 150 and 750 mM above the floor, opening must be permanently restricted to 125mm; or fitted withn a non-removable robust screen.
2-If opening between 865 and 1700mm above the floor; and no climable elements between 150 and 760mm bove the floor, opening must be restricted to 125mm; or fitted with a removable robust screen.
3- If opening between 865 of the floor; and climable elements between 150 and 760mm above the floor;or fitted with a non-removable robust screen.
4-If no opening within 1700mm of the floor. No restrictions apply.

Part 11.3.7 Protection of openable windows - bedrooms
(1) A window opening in a bedroom must be provided with protection, where the floor below the window is 2 m or more above the surface beneath.
(2) Where the lowest level of the window opening covered by (1) is less than 1.7 m above the floor, the window opening must comply with the following:
(a) The openable portion of the window must be protected with-
(i) a device capable of restricting the window opening; or
(ii) a screen with secure fittings.
(b) A device or screen required by (a) must-
(i) not permit a 125 mm sphere to pass through the window opening or screen; and
(ii) resist an outward horizontal action of 250 N against the-
(A) window restrained by a device; or
(B) screen protecting the opening; and
(iii) have a child resistant release mechanism if the screen or device is able to be removed, unlocked or overridden.
(3) Where a device or screen provided in accordance with (2)(a) is able to be removed, unlocked or overridden, a barrier with a height not less than 865 mm above the floor is required to the openable window in addition to window protection.
(4) A barrier covered by (3) must not-
(a) permit a 125 mm sphere to pass through it; and
(b) have any horizontal or near horizontal elements between 150 mm and 760 mm above the floor that facilitate climbing.

11.3.8 Protection of openable windows - rooms other than bedrooms
(1) A window opening in a room other than a bedroom must be provided with protection where the floor below the window is 4 m or more above the surface beneath.
(2) The openable part of the window covered by (a) must be protected with a barrier with a height of not less than 865mm above the floor.
(3) A barrier required by (b) must not-
(a) permit a 125 mm sphere to pass through it; and
(b) have any horizontal or near horizontal elements between 150 mm and 760 mm above the floor that facilitate climbing.

As per Section 88b Condition no. 13, No building or buildings shall be erected or permitted to remain erected on any lot burdened having a roof other than clay tiles, ceramic titles, slate or non reflective surface corrugated iron. Aslo,fence to be colorbond metal fence in Basalt color.

Bushfire Attack Level (BAL-12.5) as per report Prepared by Matthew Noone, Ref No.:-2026-00705-A, Dated :- 26-06-2026.
For full details on **BAL 12.5** - Refer Section 5 of AS3959-2018. A brief summary of some of the major construction elements are described below.

- Floor no special requirements
- Parts less than 400mm above ground or deck etc to be of Non-Combustible Material.
- External Masonry Brick walls
- Fibre cement cladding shall be minimum 6mm thickness
- Vents and weepholes shall be screened. (spark arrestors)
- 4mm Grade A Safety Glass or glass blocks within 400 mm ofground, deck etc with Openable portion metal screened withframe of metal or metal reinforced PVC-U or bushfire resisting timber
- Doors, solid timber minimum thickness 35mm for the first 400 above the threshold. Where doors incorporate glazing it shall be the same as for windows.
- Sliding doors shall be toughened glass 5mm thick minimum. Frames shall be metal or bushfire resistant timber.
- Weather strips shall be provided on garage doors
- Sarking shall comply with Planning for Bushfire Protection 2019 and be placed on top of roof framing.
- Enclosed sub floor decking to be non combustible with in 300mm horizontally and 400mm vertically from framed opening.
- Roof penetrations shall be sealed. All service pipes shall be made of metal.

Note:- this is not an exhaustive list of construction requirements for BAL 12.5. The Builder shall refer to AS3959-2018 and Planning for Bushfire Protection 2019.



NOTE
The Builder shall check all dimensions and levels on site prior to construction. Notify any errors, discrepancies or omissions to the building designer. Refer to written dimensions only. Do not scale drawings. Drawings shall not be used for construction purposes until issued for construction. This drawing reflects a design by Innovative Eco Designs and is to be used only for work when authorised in writing by Innovative Eco Designs.

All boundaries and contours are subject to survey drawing. All levels to Australian Height Data. It is the contractors responsibility to confirm all measurements on site and locations of any services prior to work on site.

All documents here within are subject to Australian Copyright Laws.



37604191460 **ABN**
(02) 8710 3852
SUITE 7, 4-10 SELEMS PDE
REVESBY, NSW,2212
design@iedesigns.com.au
www.iedesigns.com.au



A	01-07-2026	Issue for CDC

DRAWING : **Window Schedule**
CLIENT : **Sandstone Constructions**
PROJECT : **PROPOSED SINGLE STOREY DWELLING**
#12,Summer Street,Austral
Lot-2 D.P 1283987

DRAWN BY: N.B	DATE : 01-07-2026	PROJECT NO. 2605 910
SCALE:	APPLICATION : CDC	ISSUE A
PAGE SIZE A3	PAGE NO: 15	



05

PARAGON

Paragon Building Certifiers Pty Ltd

RBC00045

Registered Certifier

APPROVED

Reference: 260335/01

Date: 16/07/2026

Mail Box
1:20

All Landscape to be done by owner.

As per Section 88b Condition no. 13, No building or buildings shall be erected or permitted to remain erected on any lot burdened having a roof other than clay tiles, ceramic tiles, slate or non reflective surface corrugated iron. Aslo,fence to be colorbond metal fence in Basalt color.

LANDSCAPE SCHEDULE


Refrence Image	ABB	NAME	TYPE	HEIGHT	POT. SIZE	QUA.
	(ML)	MELALEUCA LINARIIFOLIA	Tree	8-15m	75LT.	1
	(PC)	PYRUS CALLERYANA (CHANTICLEER)	Tree	5m	45LT.	1
	(BS)	BANKSIA SPINULOSA	Shrub	1-3m	300mm	20
		BUFFALO GRASS	Grass			
		AGGREGATE				

LEGEND

Ref.img	Name
	Tree
	Shrub
	Grass (Landscape Area)
	Aggregate

GE:- GARDEN EDGING AS SELECTED TREATED PINE SPLITS 90 MM 2.4 MT LENGTH, FASTENED TO HARWOOD STAKES, MINIMUM DEPTH IN GROUND OF 300 MM WITH GALVANISED TREATED PINE SCREWS(SIZE 75 MM X 8G)

LAWN:- BUFFALO WITH SHIRLEYS NO.17 FERTILISER ALL PLANTS TO HAVE 35 MM OF BARK CHIP MULCH SPREAD OVER TOP SOIL TURF TO BE WATERED MORNING AND EVENING FOR A PERIOD OF TWO WEEKS OR AD NECESSARY.

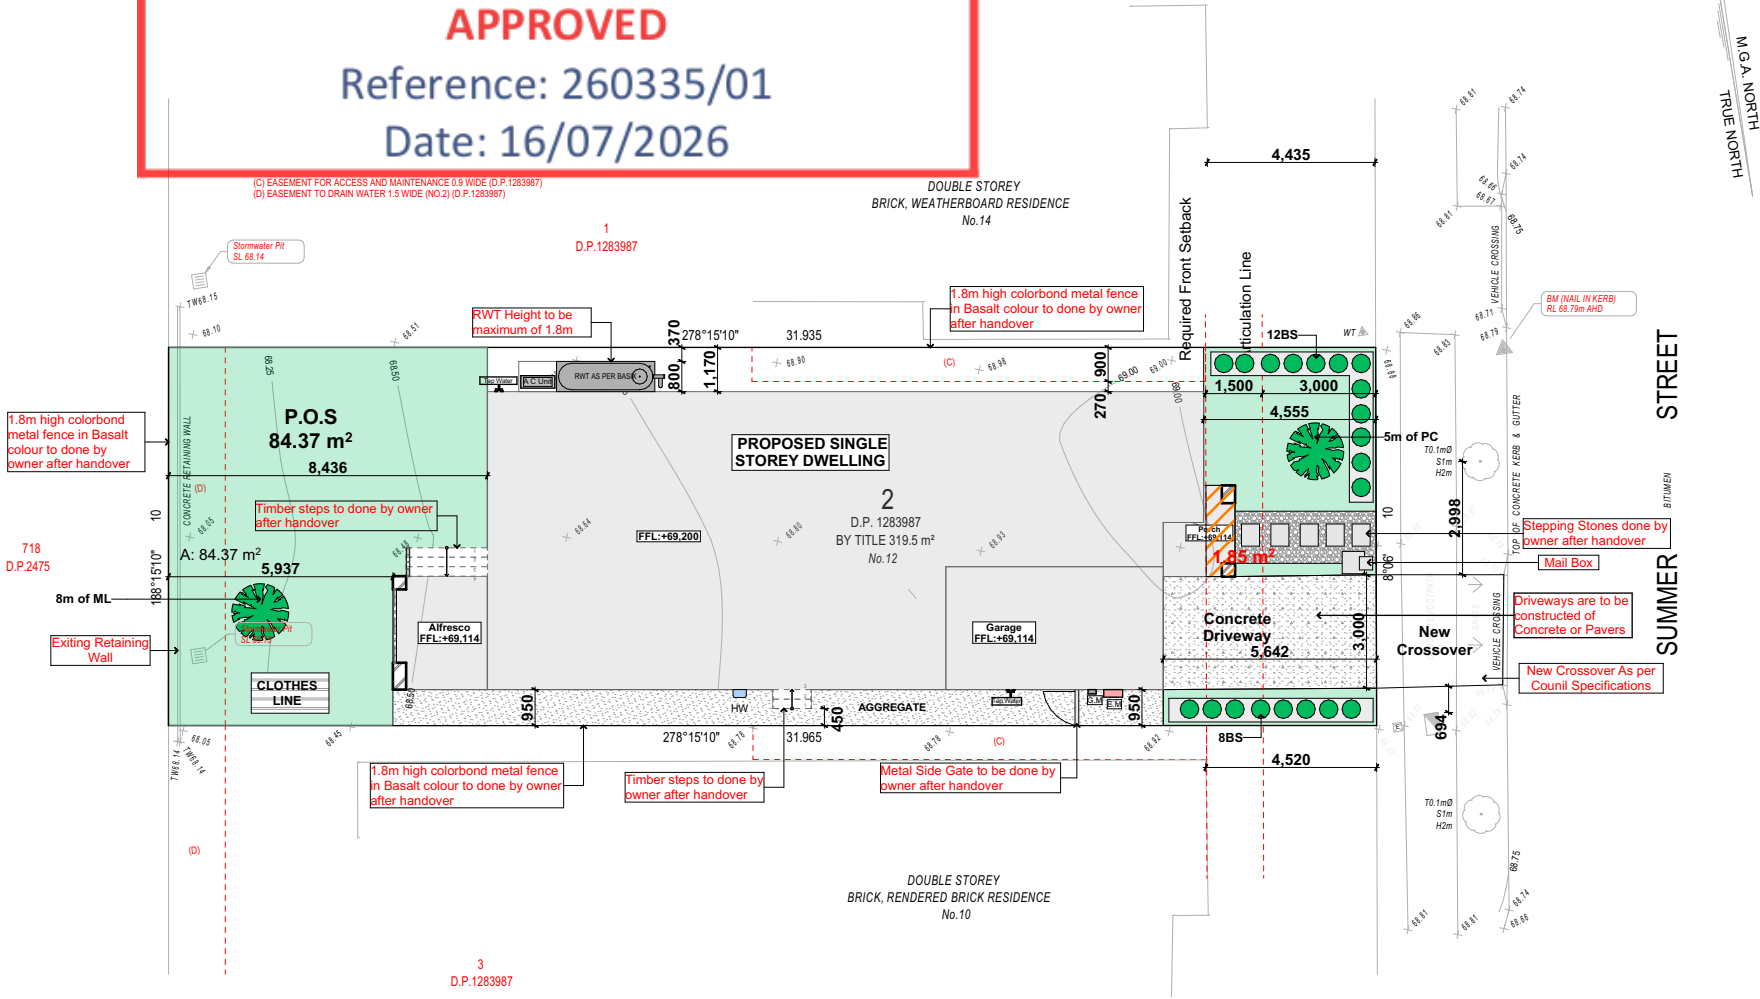

Landscape Plan
1:200



NOTE
The Builder shall check all dimensions and levels on site prior to construction. Notify any errors, discrepancies or omissions to the building designer. Refer to written dimensions only. Do not scale drawings. Drawings shall not be used for construction purposes until issued for construction. This drawing reflects a design by Innovative Eco Designs and is to be used only for work when authorised in writing by Innovative Eco Designs.

All boundaries and contours are subject to survey drawing. All levels to Australian Height Data. It is the contractors responsibility to confirm all measurements on site and locations of any services prior to work on site.


All documents here within are subject to Australian Copyright Laws.



37604191460 ABN
(02) 8710 3852
SUITE 7, 4-10 SELEMS PDE
REVESBY, NSW, 2212
design@iedesigns.com.au
www.iedesigns.com.au



A	01-07-2026	Issue for CDC

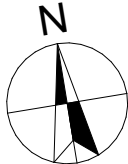

DRAWING : **Landscape Plan**

CLIENT : **Sandstone Constructions**

PROJECT : **PROPOSED SINGLE STOREY DWELLING**
#12,Summer Street,Austral
Lot-2 D.P 1283987

DRAWN BY: N.B
SCALE: 1:200
PAGE SIZE A3

DATE : **01-07-2026**
APPLICATION : CDC
PAGE NO: 16

PROJECT NO. **2605 910**
ISSUE **A**



Paragon Building Certifiers Pty Ltd


RBC00045

Registered Certifier

APPROVED

Reference: 260335/01

Date: 16/07/2026

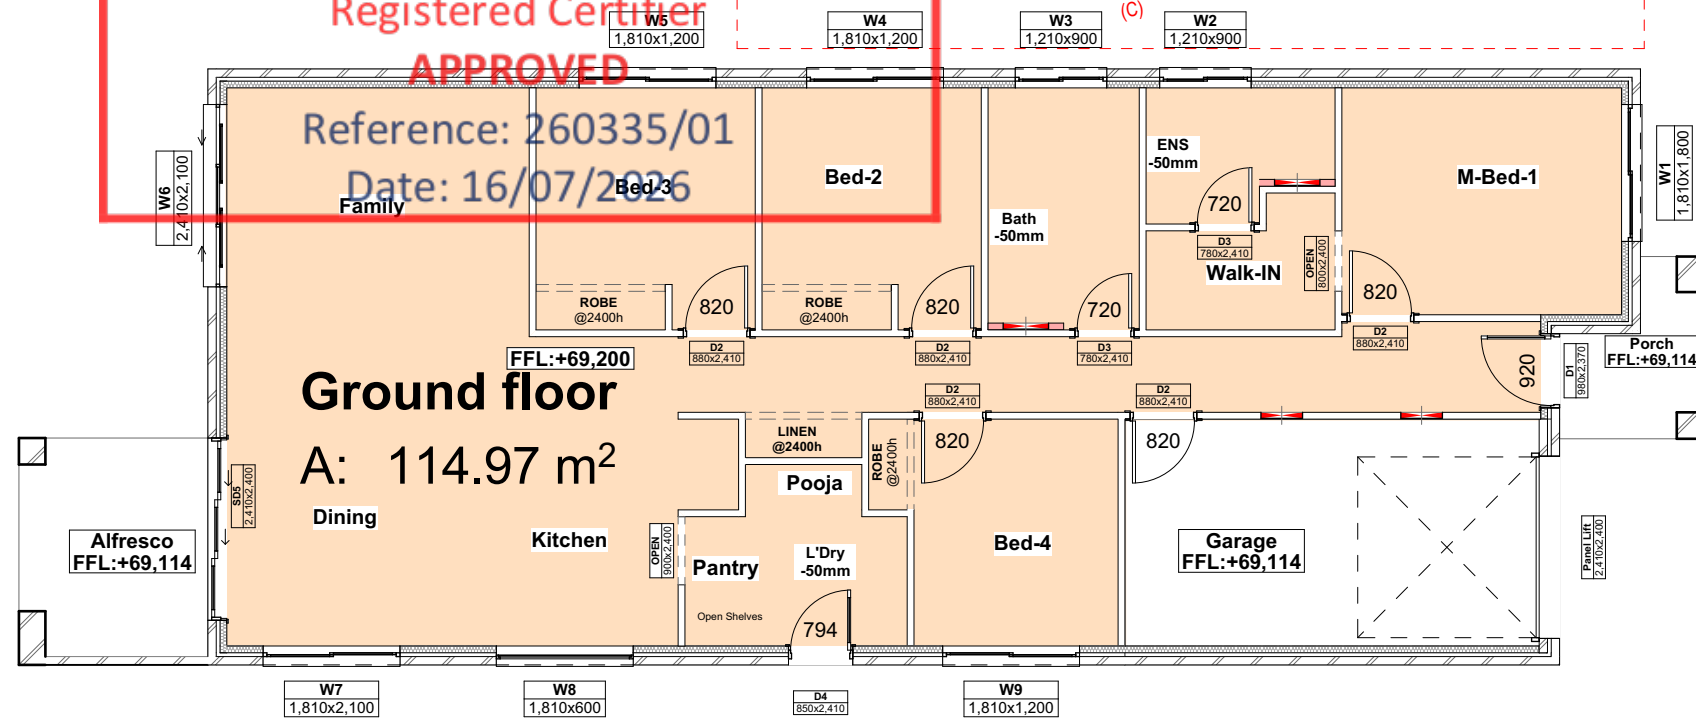

GFA -Ground Floor
1:100



NOTE
The Builder shall check all dimensions and levels on site prior to construction. Notify any errors, discrepancies or omissions to the building designer. Refer to written dimensions only. Do not scale drawings. Drawings shall not be used for construction purposes until issued for construction. This drawing reflects a design by Innovative Eco Designs and is to be used only for work when authorised in writing by Innovative Eco Designs.

All boundaries and contours are subject to survey drawing. All levels to Australian Height Data. It is the contractors responsibility to confirm all measurements on site and locations of any services prior to work on site.

All documents here within are subject to Australian Copyright Laws.



37604191460 ABN
(02) 8710 3852
SUITE 7, 4-10 SELEMS PDE
REVESBY, NSW, 2212
design@iedesigns.com.au
www.iedesigns.com.au



A	01-07-2026	Issue for CDC

DRAWING : **GFA Calculation**
CLIENT : **Sandstone Constructions**
PROJECT : **PROPOSED SINGLE STOREY DWELLING**
#12,Summer Street,Austral
Lot-2 D.P 1283987

DRAWN BY: N.B	DATE : 01-07-2026	PROJECT NO. 2605 910
SCALE: 1:100	APPLICATION : CDC	ISSUE A
PAGE SIZE A3	PAGE NO: 18	



Paragon Building Certifiers Pty Ltd


RBC00045

Registered Certifier

APPROVED

Reference: 260335/01

Date: 16/07/2026

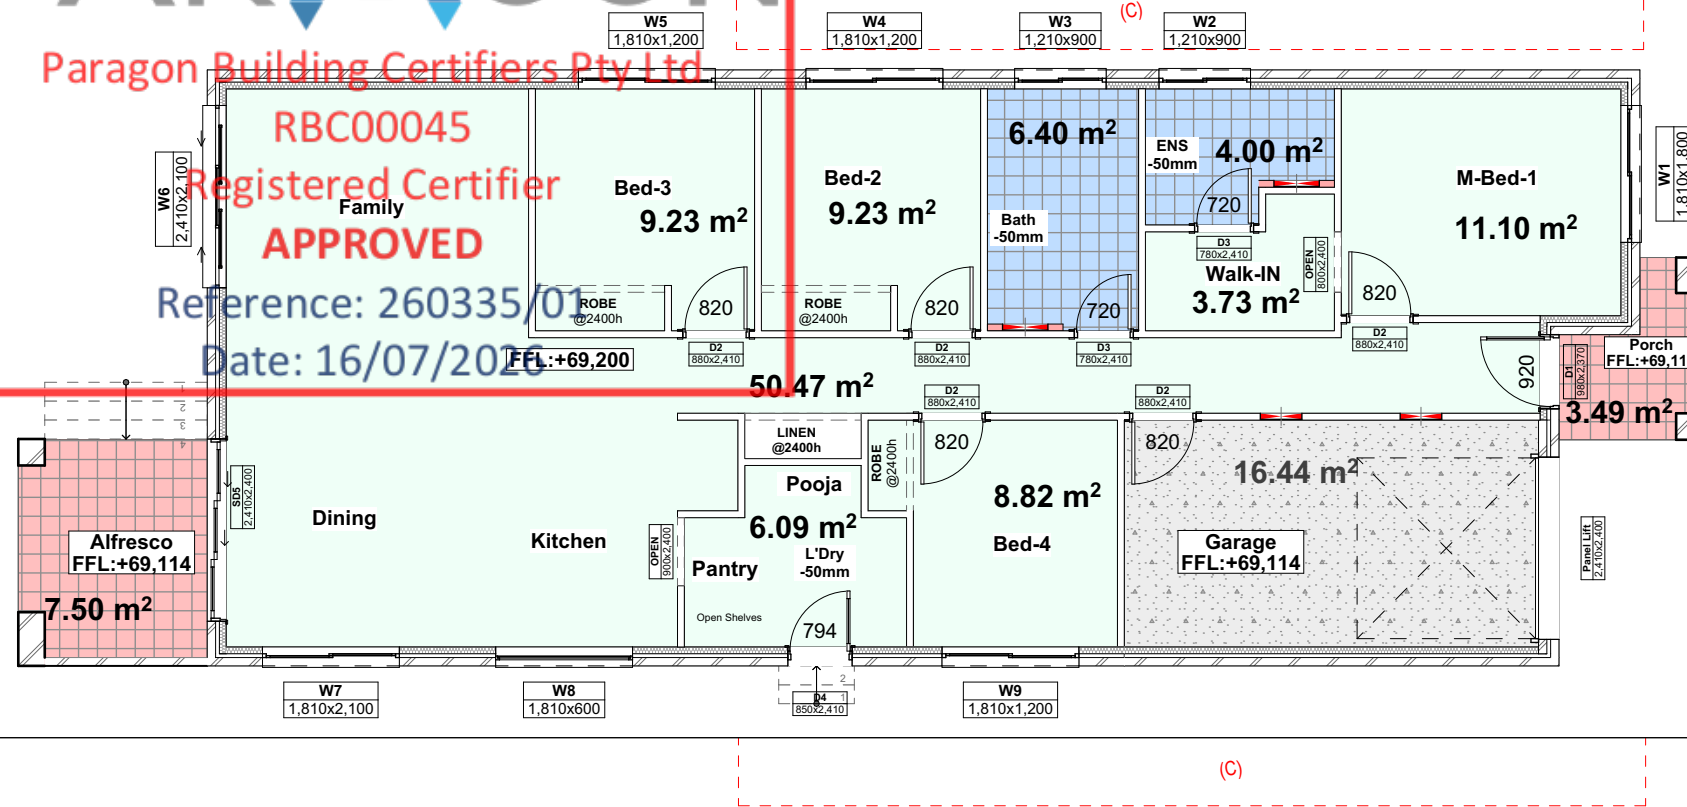

Floor Finish (Ground Floor)
1:100



NOTE
The Builder shall check all dimensions and levels on site prior to construction. Notify any errors, discrepancies or omissions to the building designer. Refer to written dimensions only. Do not scale drawings. Drawings shall not be used for construction purposes until issued for construction. This drawing reflects a design by Innovative Eco Designs and is to be used only for work when authorised in writing by Innovative Eco Designs.

All boundaries and contours are subject to survey drawing. All levels to Australian Height Data. It is the contractors responsibility to confirm all measurements on site and locations of any services prior to work on site.

All documents here within are subject to Australian Copyright Laws.



37604191460 ABN
(02) 8710 3852
SUITE 7, 4-10 SELEMS PDE
REVESBY, NSW, 2212
design@iedesigns.com.au
www.iedesigns.com.au



A	01-07-2026	Issue for CDC
---	------------	---------------

DRAWING : **Floor Finish**
CLIENT : **Sandstone Constructions**
PROJECT : **PROPOSED SINGLE STOREY DWELLING**
#12, Summer Street, Austral
Lot-2 D.P 1283987

DRAWN BY:	DATE :	PROJECT NO.
N.B	01-07-2026	2605 910
SCALE:	APPLICATION :	ISSUE
1:100	CDC	A
PAGE SIZE	PAGE NO:	
A3	19	