

PROPOSED DETACHED DUAL OCCUPANCY
42 DARTMOOR CIRCUIT EMU HEIGHTS
LOT 2033 IN DP709079



Sydney Wide Certifiers Pty Ltd
Complying Development Certificate
Reference: SWC26390/01
Date: 14/04/2026
Tristian Elyas BDC05180

DRAWING LIST	
DRAWING NUMBER	DRAWING NAME
A001	COVER PAGE
A002	NOTES
A003	BASIX CERTIFICATE
A004	AREAS
A005	SITE CONTEXT
A050	DEMOLITION PLAN
A101	SITE/GROUND FLOOR PLAN
A102	SITE/FIRST FLOOR PLAN
A103	SITE/ROOF PLAN
A201	GROUND FLOOR PLAN
A202	U2 GROUND FLOOR PLAN
A203	U1 FIRST FLOOR PLAN
A204	U2 FIRST FLOOR PLAN
A301	ELEVATIONS
A302	ELEVATIONS
A303	ELEVATIONS
A304	SECTIONS
A305	SECTIONS
A401	SCHEDULES
A402	COLOUR SCHEDULE
A403	SHADOW DIAGRAMS
A501	LANDSCAPE PLAN

SLEIMAN

PROPERTY GROUP

bdaa

ACCREDITED

BUILDING DESIGNER

BDAA Reg No. 6973

NOTE

Do not scale drawing, figured dimension only to be used.
All measurements are in millimetres.

COPYRIGHT

All rights reserved.
These drawings, plans and specifications and the copyright are the property of SLEIMAN PROPERTY GROUP and must not be used, reproduced or copied wholly or in part without the written permission of SLEIMAN PROPERTY GROUP

Northpoint

NO.	DRAWING:	BY:	DATE:	AMENDMENTS:
1	ISSUE FOR REVIEW		17/02/26	
2	ISSUE FOR CDC		13/04/26	
3				
4				
5				
6				
7				

CLIENT: DEBRA FRANCIS

ADDRESS: 42 DARTMOOR CIRCUIT EMU HEIGHTS

COVER PAGE

Project number135

DateFEB26

Drawn byLS

A001

Scale

GENERAL DEVELOPMENT NOTES:

1. POWDER COATED ALUMINIUM GUTTERS & DOWNPIPES. STORMWATER TO DISCHARGE TO STREET - REFER TO HYDRAULIC ENGINEERS PLANS (CLIENT TO DECIDE ON COLOURS & FINISHES).
2. POWDER-COATED ALUMINIUM FRAMED GLASS WINDOWS & SLIDING DOORS (CLIENT TO DECIDE ON COLOURS & FINISHES).
3. DEMOLITION & EXCAVATION TO BE CARRIED OUT BY LICENSED CONTRACTORS. FOR SEDIMENT FENCING DETAILS REFER TO 'SITE MANAGEMENT & SEDIMENT CONTROL PLAN.
4. THE DEVELOPMENT HAS BEEN DESIGNED TO BEST MEET THE GUIDELINES OF COUNCIL & THE B.C.A (ALL WORK ON SITE SHALL SIMILARLY BE CARRIED OUT TO ADHERE TO THE REQUIREMENTS OF LOCAL COUNCIL AND THE B.C.A).
5. ALL PORCH'S, GARAGES, VERANDAHS, BALCONIES & THE LIKE TO HAVE A MINIMUM 85mm STEPDOWN. (ENGINEERS DETAILS TO SUPERCEED).
6. BITUMOUS MASONRY ARTICULATION JOINTS ON UNARTICULATED WALLS WITH LENGTHS GREATER THAN 6m TO BE LOCATED BEHIND DOWNPIPE LOCATIONS WHERE PRACTICAL.
7. ALL BALUSTRADES TO BE A MINIMUM 1000mm ABOVE FINISHED FLOOR LEVEL RAILS TO BE SPACED SO AS TO PREVENT A 125mm SPHERE PENETRATING THROUGH.
8. BALCONIES TO BE SUITABLY WATERPROOFED & GRADED TO SUIT THE REQUIREMENTS OF THE B.C.A.
9. ALL BATHROOM, ENSUITES, LAUNDRIES AND BALCONIES (ENCLOSED) TO HAVE FLOOR WASTES, BE SETDOWN AND WATERPROOFED.
10. LAND TO BATTER AS SHOWN WITH A SOLID GROUND LINE (EXISTING GROUND LEVELS SHOWN DASHED) MAXIMUM BATTER ON STABLE GROUND NOT TO EXCEED 1 IN 4 (IN WHICH CASE RETAINING WALLS ARE TO BE INCORPORATED - TO ENGINEERS SPECIFICATIONS).

GENERAL CONSTRUCTION NOTES:

1. THESE DRAWINGS SHALL BE READ IN CONJUNCTION WITH ALL ARCHITECTURAL AND OTHER CONSULTANT'S DRAWINGS AND SPECIFICATIONS AND WITH SUCH OTHER WRITTEN INSTRUCTIONS AS MAY BE ISSUED DURING THE COURSE OF THE CONTRACT. ALL DISCREPANCIES SHALL BE REFERRED TO THE CONTRACT ALL DISCREPANCIES SHALL BE REFERRED TO THE ARCHITECT FOR A DECISION BEFORE PROCEEDING WITH THE WORK.
2. ALL DIMENSIONS RELEVANT TO SETTING OUT AND OFF-SITE WORK SHALL BE VERIFIED BY THE CONTRACTOR BEFORE CONSTRUCTION AND FABRICATION IS COMMENCED. THE ARCHITECTURAL DRAWINGS SHALL NOT BE SCALED.
3. DURING CONSTRUCTION THE CONTRACTOR SHALL BE RESPONSIBLE FOR MAINTAINING THE STRUCTURE IN A STABLE CONDITION AND ENSURING NO PART SHALL BE OVERSTRESSED UNDER CONSTRUCTION ACTIVITIES. TEMPORARY BRACING SHALL BE PROVIDED BY THE CONTRACTOR AS REQUIRED.
4. ALL WORKMANSHIP AND MATERIALS ARE TO BE IN ACCORDANCE WITH THE RELEVANT CURRENT S.A.A. CODES INCLUDING ALL AMENDMENTS, AND THE LOCAL STATUTORY AUTHORITIES, REGULATIONS, ETC., EXCEPT WHERE VARIED BY THE CONTRACT DOCUMENTS.
5. THE APPROVAL OF A SUBSTITUTION SHALL BE SOUGHT FROM THE ENGINEER,BUT IS NOT AN AUTHORISATION FOR AN EXTRA. ANY EXTRA INVOLVED MUST BE VERIFIED WITH THE ARCHITECT BEFORE THE WORK COMMENCES.
6. ALL DIMENSIONS ARE IN MILLIMETRES UNLESS STATED OTHERWISE. ALL LEVELS ARE EXPRESSED IN METRES TO AHD.
7. SETTING-OUT DIMENSIONS AND SIZES OF STRUCTURAL MEMBERS SHALL NOT BE OBTAINED BY SCALING THE STRUCTURAL DRAWINGS. ANY SETTING-OUT DIMENSIONS SHOWN IN THE STRUCTURAL DRAWINGS SHALL BE CHECKED BY THE CONTRACTOR BEFORE CONSTRUCTION COMMENCES.
8. DURING THE ALTERATION, THE EXISTING BUILDING SHALL BE PROTECTED ESPECIALLY FROM THE RAIN.
9. WORKMANSHIP, QUALITY AND STANDARDS OF WORK SHALL FOLLOW THE NEW SOUTH WALES GUIDE TO STANDARD AND TOLERANCES 2017.

SCHEDULE OF AUSTRALIAN STANDARD TO BE FOLLOWED:

1. AS 1288 - GLASS IN BUILDINGS, SELECTION & INSTALLATION.
2. AS/NZS 1170 - STRUCTURAL DESIGN ACTIONS.
3. AS 1562 - DESIGN & INSTALLATION OF SHEET ROOF & WALL CLADDING, METAL.
4. AS/NZS - DESIGN & INSTALLATION OF SHEET ROOF & WALL CLADDING, CORRUGATED FIRBE-REINFORCED CEMENT & PLASTICS.
5. AS 1668 - THE USE OF MECHANICAL VENTILATION & AIR CONDITIONING IN BUILDINGS.
6. AS/NZS 1680 - INTERIOR LIGHTING & SAFE MOVEMENT
7. AS 1684 - RESIDENTIAL TIMBER-FRAMED CONSTRUCTION.
8. AS 1926 - SWIMMING POOL SAFETY.
9. AS 2047 - WINDOWS IN BUILDINGS, SELECTION & INSTALLATION.
10. AS 2049 - ROOF TILES.
11. AS 2050 - INSTALLATION OF ROOF TILES.
12. AS/NZS 2269 - PLYWOOD, STRUCTURAL SPECIFICATIONS.
13. AS 2870 - RESIDENTIAL SLABS & FOOTINGS CONSTRUCTION.
14. AS/NZS 2904 - DAMP-PROOF COURSES & FLASHINGS.
15. AS/NZS 3500 - PLUMBING & DRAINAGE, STORMWATER DRAINAGE, HEATED SERVICES & DOMESTIC INSTALLATIONS.
16. AS 3600 - CONCRETE STRUCTURES.
17. AS 3660 - TERMITE MANAGEMENT.
18. AS 3700 - MASONRY STRUCTURES.
19. AS 3740 - WATERPROOFING OF WET AREAS IN RESIDENTIAL BUILDINGS.
20. AS 3786 - SMOKE ALARMS.
21. AS 3959 - CONSTRUCTION OF BUILDINGS IN BUSHFIRE-PRONE AREAS.
22. AS 4055 - WIND LOADS FOR HOUSING.
23. AS 4100 - STEEL STRUCTURES.
24. AS/NZS 4200 - PLIABLE BUILDING MEMBRANES & UNDERLAYS, MATERIALS & INSTALLATION REQUIREMENTS.
25. AS 4254 - DUCKWORK FOR AIR-HANDLING SYSTEMS IN BUILDINGS.
26. AS/NZS - 4600 - COLD-FORMED STEEL STRUCTURES.
27. AS 4773 - MASONRY FOR SMALL BUILDINGS, DESIGN & CONSTRUCTION.
28. AS/NZS 4858 - WET AREA MEMBRANES.
29. AS3000 ELECTRICAL INSTALLATIONS.
30. AS3008 ELECTRICAL INSTALLATIONS - SELECTION OF CABLES.
31. AS/NZS 3017 ELECTRICAL INSTALLATIONS - VERIFICATION GUIDELINES.
32. AS/NZS 3100 APPROVAL AND TEST SPECIFICATION - GENERAL REQUIREMENTS FOR ELECTRICAL EQUIPMENT.
33. AS 4586-2013 SLIP RESISTANCE CLASSIFICATION OF NEW PEDESTRIAN SURFACE MATERIAL (CLASS P2 FOR TILES IN BATHROOM, TOILET, AND KITCHEN)

GENERAL NOTES

- SMOKE ALARMS ARE TO BE INSTALLED IN ACCORDANCE WITH AS3786-1993. ALARMS ARE TO BE POSITIONED ON THE CEILING AND SETBACK A MINIMUM DISTANCE OF 300mm FROM ANY WALL.
- WET AREAS ARE TO BE WATERPROOFED IN ACCORDANCE WITH AS3740 WATERPROOFING OF WET AREAS WITHIN ALL GLAZING TO COMPLY WITH AS 1288 - "GLASS IN BUILDING".
- ALL BUILDING WORK AND CONSTRUCTION MATERIALS TO COMPLY WITH BUILDING CODE OF AUSTRALIA STANDARDS
- STAIR CASES TO INTERNALS OF BUILDING TO HAVE 187.5MM RISER & 250MM GOINGS TO COMPLY WITH BUILDING CODE OF AUSTRALIA STANDARDS.



1. FALLS, SLIPS, TRIPS

a) WORKING AT HEIGHTS

DURING CONSTRUCTION

Wherever possible, components for this building should be prefabricated off-site or at ground level to minimise the risk of workers falling more than two metres. However, construction of this building will require workers to be working at heights where a fall in excess of two metres is possible and injury is likely to result from such a fall. The builder should provide a suitable barrier wherever a person is required to work in a situation where falling more than two metres is a possibility.

DURING OPERATION OR MAINTENANCE

For houses or other low-rise buildings where scaffolding is appropriate:

Cleaning and maintenance of windows, walls, roof or other components of this building will require persons to be situated where a fall from a height in excess of two metres is possible. Where this type of activity is required, scaffolding, ladders or trestles should be used in accordance with relevant codes of practice, regulations or legislation.

For buildings where scaffold, ladders, trestles are not appropriate: Cleaning and maintenance of windows, walls, roof or other components of this building will require persons to be situated where a fall from a height in excess of two metres is possible. Where this type of activity is required, scaffolding, fall barriers or Personal Protective Equipment (PPE) should be used in accordance with relevant codes of practice, regulations or legislation.

ANCHORAGE POINTS

Anchorage points for portable scaffold or fall arrest devices have been included in the design for use by maintenance workers. Any persons engaged to work on the building after completion of construction work should be informed about the anchorage points.

b) SLIPPERY OR UNEVEN SURFACES

FLOOR FINISHES Specified

If finishes have been specified by designer, these have been selected to minimise the risk of floors and paved areas becoming slippery when wet or when walked on with wet shoes/feet. Any changes to the specified finish should be made in consultation with the designer or, if this is not practical, surfaces with an equivalent or better slip resistance should be chosen.

FLOOR FINISHES By Owner

If designer has not not been involved in the selection of surface finishes, the owner is responsible for the selection of surface finishes in the pedestrian trafficable areas of this building. Surfaces should be selected in accordance with AS HB 197:1999 and AS/NZ 4586:2004.

STEPS, LOOSE OBJECTS AND UNEVEN SURFACES

Due to design restrictions for this building, steps and/or ramps are included in the building which may be a hazard to workers carrying objects or otherwise occupied. Steps should be clearly marked with both visual and tactile warning during construction, maintenance, demolition and at all times when the building operates as a workplace.

Building owners and occupiers should monitor the pedestrian access ways and in particular access to areas where maintenance is routinely carried out to ensure that surfaces have not moved or cracked so that they become uneven and present a trip hazard. Spills, loose material, stray objects or any other matter that may cause a slip or trip hazard should be cleaned or removed from access ways.

Contractors should be required to maintain a tidy work site during construction, maintenance or demolition to reduce the risk of trips and falls in the workplace. Materials for construction or maintenance should be stored in designated areas away from access ways and work areas.

2. FALLING OBJECTS

LOOSE MATERIALS OR SMALL OBJECTS

Construction, maintenance or demolition work on or around this building is likely to involve persons working above ground level or above floor levels. Where this occurs one or more of the following measures should be taken to avoid objects falling from the area where the work is being carried out onto persons below.

1. Prevent or restrict access to areas below where the work is being carried out.
2. Provide toeboards to scaffolding or work platforms.
3. Provide protective structure below the work area.
4. Ensure that all persons below the work area have Personal Protective Equipment (PPE).

BUILDING COMPONENTS

During construction, renovation or demolition of this building, parts of the structure including fabricated steelwork, heavy panels and many other components will remain standing prior to or after supporting parts are in place. Contractors should ensure that temporary bracing or other required support is in place at all times when collapse which may injure persons in the area is a possibility.

Mechanical lifting of materials and components during construction, maintenance or demolition presents a risk of falling objects. Contractors should ensure that appropriate lifting devices are used, that loads are properly secured and that access to areas below the load is prevented or restricted.

3. TRAFFIC MANAGEMENT

For building on a major road, narrow road or steeply sloping road: Parking of vehicles or loading/unloading of vehicles on this roadway may cause a traffic hazard. During construction, maintenance or demolition of this building designated parking for workers and loading areas should be provided. Trained traffic management personnel should be responsible for the supervision of these areas.

For building where on-site loading/unloading is restricted:

Construction of this building will require loading and unloading of materials on the roadway. Deliveries should be well planned to avoid congestion of loading areas and trained traffic management personnel should be used to supervise loading/unloading areas.

For all buildings:

Busy construction and demolition sites present a risk of collision where deliveries and other traffic are moving within the site. A traffic management plan supervised by trained traffic management personnel should be adopted for the work site.

4. SERVICES

GENERAL

Rupture of services during excavation or other activity creates a variety of risks including release of hazardous material. Existing services are located on or around this site. Where known, these are identified on the plans but the exact location and extent of services may vary from that indicated. Services should be located using an appropriate service (such as Dial Before You Dig), appropriate excavation practice should be used and, where necessary, specialist contractors should be used.

Locations with underground power:

Underground power lines MAY be located in or around this site. All underground power lines must be disconnected or carefully located and adequate warning signs used prior to any construction, maintenance or demolition commencing.

Locations with overhead power lines:

Overhead power lines MAY be near or on this site. These pose a risk of electrocution if struck or approached by lifting devices or other plant and persons working above ground level. Where there is a danger of this occurring, power lines should be, where practical, disconnected or relocated. Where this is not practical adequate warning in the form of bright coloured tape or signage should be used or a protective barrier provided.

5. MANUAL TASKS

Components within this design with a mass in excess of 25kg should be lifted by two or more workers or by mechanical lifting device. Where this is not practical, suppliers or fabricators should be required to limit the component mass.

All material packaging, building and maintenance components should clearly show the total mass of packages and where practical all items should be stored on site in a way which minimises bending before lifting. Advice should be provided on safe lifting methods in all areas where lifting may occur. Construction, maintenance and demolition of this building will require the use of portable tools and equipment. These should be fully maintained in accordance with manufacturer's specifications and not used where faulty or (in the case of electrical equipment) not carrying a current electrical safety tag. All safety guards or devices should be regularly checked and Personal Protective Equipment should be used in accordance with manufacturer's specification.

6. HAZARDOUS SUBSTANCES

ASBESTOS

For alterations to a building constructed prior to 1990:

If this existing building was constructed prior to:

1990 - it therefore may contain asbestos

1986 - it therefore is likely to contain asbestos either in cladding material or in fire retardant insulation material. In either case, the builder should check and, if necessary, take appropriate action before demolishing, cutting, sanding, drilling or otherwise disturbing the existing structure.

POWDERED MATERIALS

Many materials used in the construction of this building can cause harm if inhaled in powdered form. Persons working on or in the building during construction, operational maintenance or demolition should ensure good ventilation and wear Personal Protective Equipment including protection against inhalation while using powdered material or when sanding, drilling, cutting or otherwise disturbing or creating powdered material.

TREATED TIMBER

The design of this building may include provision for the inclusion of treated timber within the structure. Dust or fumes from this material can be harmful. Persons working on or in the building during construction, operational maintenance or demolition should ensure good ventilation and wear Personal Protective Equipment including protection against inhalation of harmful material when sanding, drilling, cutting or using treated timber in any way that may cause harmful material to be released. Do not burn treated timber.

VOLATILE ORGANIC COMPOUNDS

Many types of glue, solvents, spray packs, paints, varnishes and some cleaning materials and disinfectants have dangerous emissions. Areas where these are used should be kept well ventilated while the material is being used and for a period after installation. Personal Protective Equipment may also be required. The manufacturer's recommendations for use must be carefully considered at all times.

SYNTHETIC MINERAL FIBRE

Fibreglass, rockwool, ceramic and other material used for thermal or sound insulation may contain synthetic mineral fibre which may be harmful if inhaled or if it comes in contact with the skin, eyes or other sensitive parts or the body. Personal Protective Equipment including protection against inhalation of harmful material should be used when installing, removing or working near bulk insulation material.

TIMBER FLOORS

This building may contain timber floors which have an applied finish. Areas where finishes are applied should be kept well ventilated during sanding and application and for a period after installation. Personal Protective Equipment may also be required. The manufacturer's recommendations for use must be carefully considered at all times.

7. CONFINED SPACES

EXCAVATION

Construction of this building and some maintenance on the building will require excavation and installation of items within excavations. Where practical, installation should be carried out using methods which do not require workers to enter the excavation. Where this is not practical, adequate support for the excavated area should be provided to prevent collapse. Warning signs and barriers to prevent accidental or unauthorised access to all excavations should be provided.

ENCLOSED SPACES

For buildings with enclosed spaces where maintenance or other access may be required:

Enclosed spaces within this building may present a risk to persons entering for construction, maintenance or any other purpose. The design documentation calls for warning signs and barriers to unauthorised access. These should be maintained throughout the life of the building. Where workers are required to enter enclosed spaces, air testing equipment and Personal Protective Equipment should be provided.

SMALL SPACES

For buildings with small spaces where maintenance or other access may be required:

Some small spaces within this building will require access by construction or maintenance workers. The design documentation calls for warning signs and barriers to unauthorised access. These should be maintained throughout the life of the building. Where workers are required to enter small spaces they should be scheduled so that access is for short periods. Manual lifting and other manual activity should be restricted in small spaces.

8. PUBLIC ACCESS

Public access to construction and demolition sites and to areas under maintenance causes risk to workers and public. Warning signs and secure barriers to unauthorised access should be provided. Where electrical installations, excavations, plant or loose materials are present they should be secured when not fully supervised.

9. OPERATIONAL USE OF BUILDING RESIDENTIAL BUILDINGS

This building has been designed as a residential building. If, at a later date, it is used or intended to be used as a workplace, the provisions of the Work Health and Safety Act 2011 or subsequent replacement Act should be applied to the new use.

NON-RESIDENTIAL BUILDINGS

For non-residential buildings where the end-use has not been identified:

This building has been designed to requirements of the classification identified on the drawings. The specific use of the building is not known at the time of the design and a further assessment of the workplace health and safety issues should be undertaken at the time of fit-out for the end-user.

For non-residential buildings where the end-use is known:

This building has been designed for the specific use as identified on the drawings. Where a change of use occurs at a later date a further assessment of the workplace health and safety issues should be undertaken.

10.OTHER HIGH RISK ACTIVITY

All electrical work should be carried out in accordance with Code of Practice: Managing Electrical Risks at the Workplace, AS/NZ 3012 and all licensing requirements.

All work using Plant should be carried out in accordance with Code of Practice: Managing Risks of Plant at the Workplace.

All work should be carried out in accordance with Code of Practice: Managing Noise and Preventing Hearing Loss at Work.

Due to the history of serious incidents it is recommended that particular care be exercised when undertaking work involving steel construction and concrete placement. All the above applies.

keep one of these #9 notes, as appropriate

SLEIMAN
PROPERTY GROUP

bdaa
ACCREDITED
BUILDING DESIGNER

BDAA Reg No. 6973

NOTE

Do not scale drawing, figured dimension only to be used. All measurements are in millimetres.

COPYRIGHT

All rights reserved.

These drawings, plans and specifications and the copyright are the property of SLEIMAN PROPERTY GROUP and must not be used, reproduced or copied wholly or in part without the written permission of SLEIMAN PROPERTY GROUP

Northpoint



NO.	DRAWING:	BY:	DATE:	AMENDMENTS:
1	ISSUE FOR REVIEW		17/02/26	
2	ISSUE FOR CDC		13/04/26	
3				
4				
5				
6				
7				

CLIENT:	DEBRA FRANCIS	NOTES										
ADDRESS:	42 DARTMOOR CIRCUIT EMU HEIGHTS	<table><tr><td>Project number</td><td>135</td><td rowspan="3">A002</td></tr><tr><td>Date</td><td>FEB26</td></tr><tr><td>Drawn by</td><td>LS</td></tr><tr><td></td><td></td><td>Scale</td></tr></table>	Project number	135	A002	Date	FEB26	Drawn by	LS			Scale
Project number	135	A002										
Date	FEB26											
Drawn by	LS											
		Scale										

BASIX CERTIFICATE
Multi Dwelling
Certificate number: 1841651M

(i) Water	Show on DA plans	Show on CC/CDC plans & specs	Certifier check
(a) The applicant must comply with the commitments listed below in carrying out the development of a dwelling listed in a table below.			
(b) The applicant must plant indigenous or low water use species of vegetation throughout the area of land specified for the dwelling in the "Indigenous species" column of the table below, as private landscaping for that dwelling. (This area of indigenous vegetation is to be contained within the "Area of garden and lawn" for the dwelling specified in the "Description of Project" table).	✓	✓	
(c) If a rating is specified in the table below for a fixture or appliance to be installed in the dwelling, the applicant must ensure that each such fixture and appliance meets the rating specified for it.		✓	✓
(d) The applicant must install an on demand hot water recirculation system which regulates all hot water use throughout the dwelling, where indicated for a dwelling in the "HW recirculation or diversion" column of the table below.		✓	✓
(e) The applicant must install: (aa) a hot water diversion system to all showers, kitchen sinks and all basins in the dwelling, where indicated for a dwelling in the "HW recirculation or diversion" column of the table below; and (bb) a separate diversion tank (or tanks) connected to the hot water diversion systems of at least 100 litres. The applicant must connect the hot water diversion tank to all toilets in the dwelling.		✓ ✓	✓ ✓
(e) The applicant must not install a private swimming pool or spa for the dwelling, with a volume exceeding that specified for it in the table below.	✓	✓	
(f) If specified in the table, that pool or spa (or both) must have a pool cover or shading (or both).		✓	
(g) The pool or spa must be located as specified in the table.	✓	✓	
(h) The applicant must install, for the dwelling, each alternative water supply system, with the specified size, listed for that dwelling in the table below. Each system must be configured to collect run-off from the areas specified (excluding any area which supplies any other alternative water supply system), and to divert overflow as specified. Each system must be connected as specified.	✓	✓	✓

(ii) Energy	Show on DA plans	Show on CC/CDC plans & specs	Certifier check
(a) The applicant must comply with the commitments listed below in carrying out the development of a dwelling listed in a table below.			
(b) The applicant must install each hot water system specified for the dwelling in the table below, so that the dwelling's hot water is supplied by that system. If the table specifies a central hot water system for the dwelling, then the applicant must connect that central system to the dwelling, so that the dwelling's hot water is supplied by that central system.	✓	✓	✓
(c) The applicant must install, in each bathroom, kitchen and laundry of the dwelling, the ventilation system specified for that room in the table below. Each such ventilation system must have the operation control specified for it in the table.		✓	✓
(d) The applicant must install the cooling and heating system/s specified for the dwelling under the "Living areas" and "Bedroom areas" headings of the "Cooling" and "Heating" columns in the table below, in/for at least 1 living/bedroom area of the dwelling. If no cooling or heating system is specified in the table for "Living areas" or "Bedroom areas", then no systems may be installed in any such areas. If the term "zoned" is specified beside an air conditioning system, then the system must provide for day/night zoning between living areas and bedrooms.		✓	✓

(ii) Energy	Show on DA plans	Show on CC/CDC plans & specs	Certifier check
(e) This commitment applies to each room or area of the dwelling which is referred to in a heading to the "Artificial lighting" column of the table below (but only to the extent specified for that room or area). The applicant must ensure that the "primary type of artificial lighting" for each such room in the dwelling is fluorescent lighting or light emitting diode (LED) lighting. If the term "dedicated" is specified for a particular room or area, then the light fittings in that room or area must only be capable of being used for fluorescent lighting or light emitting diode (LED) lighting.		✓	✓
(f) This commitment applies to each room or area of the dwelling which is referred to in a heading to the "Natural lighting" column of the table below (but only to the extent specified for that room or area). The applicant must ensure that each such room or area is fitted with a window and/or skylight.		✓	✓
(g) This commitment applies if the applicant installs a water heating system for the dwelling's pool or spa. The applicant must: (aa) install the system specified for the pool in the "Individual Pool" column of the table below (or alternatively must not install any system for the pool). If specified, the applicant must install a timer, to control the pool's pump; and (bb) install the system specified for the spa in the "Individual Spa" column of the table below (or alternatively must not install any system for the spa). If specified, the applicant must install a timer to control the spa's pump.		✓ BDC05180	✓
(h) The applicant must install in the dwelling: (aa) the kitchen cook-top and oven specified for that dwelling in the "Appliances & other efficiency measures" column of the table below; (bb) each appliance for which a rating is specified for that dwelling in the "Appliances & other efficiency measures" column of the table, and ensure that the appliance has that minimum rating; and (cc) any clothes drying line specified for the dwelling in the "Appliances & other efficiency measures" column of the table.		✓ ✓ ✓	✓
(i) If specified in the table, the applicant must carry out the development so that each refrigerator space in the dwelling is "well ventilated".		✓	
(j) The applicant must install the photovoltaic system specified for the dwelling under the "Photovoltaic system" heading of the "Alternative energy" column of the table below, and connect the system to that dwelling's electrical system.	✓	✓	✓

(iii) Thermal Performance and Materials	Show on DA plans	Show on CC/CDC plans & specs	Certifier check
(d) The applicant must show on the plans accompanying the development application for the proposed development, all matters which the Thermal Comfort Protocol requires to be shown on those plans. Those plans must bear a stamp of endorsement from the Accredited Assessor, to certify that this is the case.	✓		
(e) The applicant must show on the plans accompanying the application for a construction certificate (or complying development certificate, if applicable), all thermal performance specifications set out in the Assessor Certificate, and all aspects of the proposed development which were used to calculate those specifications.		✓	
(f) The applicant must construct the development in accordance with all thermal performance specifications set out in the Assessor Certificate, and in accordance with those aspects of the development application or application for a complying development certificate which were used to calculate those specifications.		✓	✓
(g) Where there is an in-slab heating or cooling system, the applicant must: (aa) Install insulation with an R-value of not less than 1.0 around the vertical edges of the perimeter of the slab; or (bb) On a suspended floor, install insulation with an R-value of not less than 1.0 underneath the slab and around the vertical edges of the perimeter of the slab.	✓	✓	✓
(h) The applicant must construct the floors and walls of the development in accordance with the specifications listed in the table below.	✓	✓	✓
(i) The applicant must show on The plans accompanying The development application for The proposed development, The locations of ceiling fans set out in The Assessor Certificate.	✓		
(j) The applicant must show on the plans accompanying the application for a construction certificate (or complying development certificate, if applicable), the locations of ceiling fans set out in the Assessor Certificate.		✓	

(i) Water	Show on DA plans	Show on CC/CDC plans & specs	Certifier check
(a) If, in carrying out the development, the applicant installs a showerhead, toilet, tap or clothes washer into a common area, then that item must meet the specifications listed for it in the table.		✓	✓
(b) The applicant must install (or ensure that the development is serviced by) the alternative water supply system(s) specified in the "Central systems" column of the table below. In each case, the system must be sized, be configured, and be connected, as specified in the table.	✓	✓	✓
(c) A swimming pool or spa listed in the table must not have a volume (in kLs) greater than that specified for the pool or spa in the table.	✓	✓	
(d) A pool or spa listed in the table must have a cover or shading if specified for the pool or spa in the table.		✓	
(e) The applicant must install each fire sprinkler system listed in the table so that the system is configured as specified in the table.		✓	✓
(f) The applicant must ensure that the central cooling system for a cooling tower is configured as specified in the table.		✓	✓

Common area	Showerheads rating	Toilets rating	Taps rating	Clothes washers rating
All common areas	no common facility	no common facility	no common facility	no common laundry facility

(ii) Energy	Show on DA plans	Show on CC/CDC plans & specs	Certifier check
(a) If, in carrying out the development, the applicant installs a ventilation system to service a common area specified in the table below, then that ventilation system must be of the type specified for that common area, and must meet the efficiency measure specified.		✓	✓
(b) In carrying out the development, the applicant must install, as the "primary type of artificial lighting" for each common area specified in the table below, the lighting specified for that common area. This lighting must meet the efficiency measure specified. The applicant must also install a centralised lighting control system or Building Management System (BMS) for the common area, where specified.		✓	✓
(c) The applicant must install the systems and fixtures specified in the "Central energy systems" column of the table below. In each case, the system or fixture must be of the type, and meet the specifications, listed for it in the table.	✓	✓	✓



NO.	DRAWING:	BY:	DATE:	AMENDMENTS:
1	ISSUE FOR REVIEW		17/02/26	
2	ISSUE FOR CDC		13/04/26	
3				
4				
5				
6				
7				

CLIENT: **DEBRA FRANCIS**

BASIX CERTIFICATE

ADDRESS: **42 DARTMOOR CIRCUIT EMU HEIGHTS**


Project number 135

Date FEB26

Drawn by LS


A003

Scale

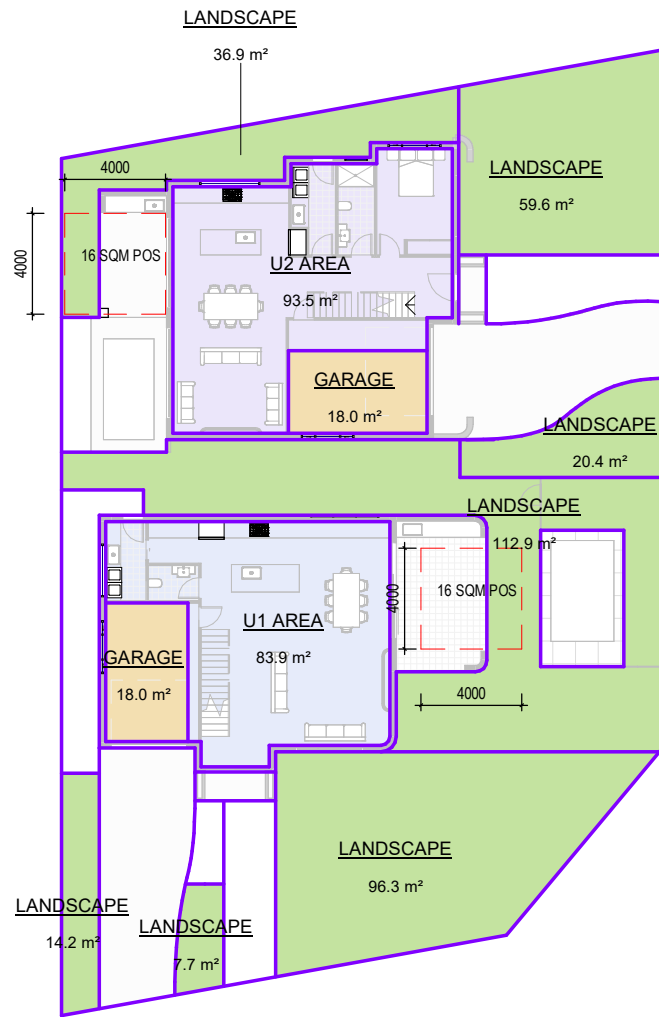

GROUND FLOOR

1 : 300

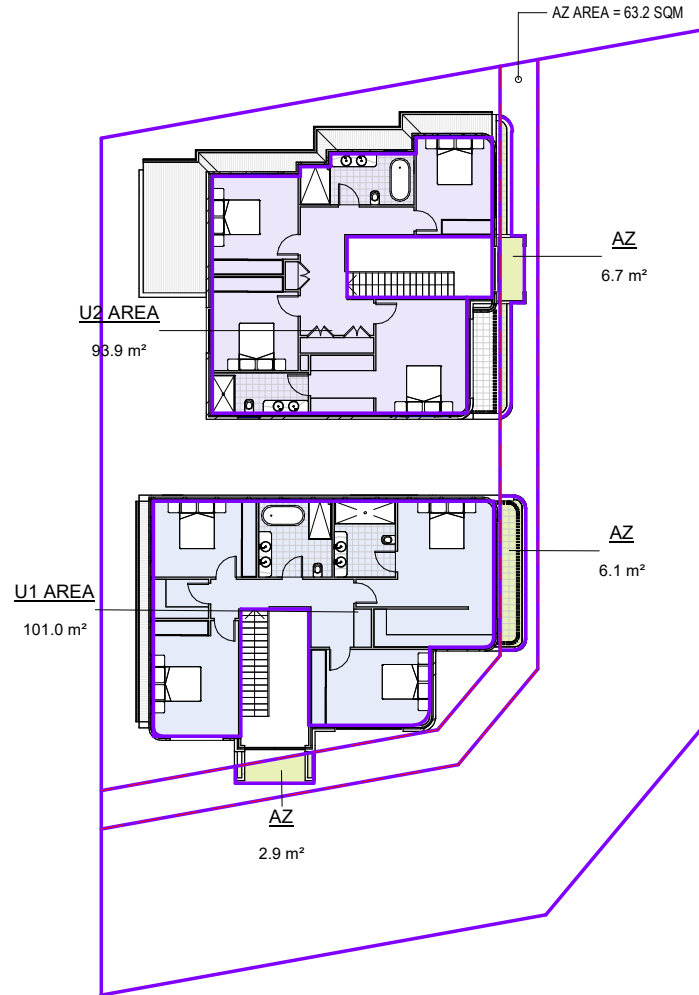

FIRST FLOOR

Sydney Wide Certifiers Pty Ltd
Complying Development Certificate
Reference: SWC26390/01
Date: 14/04/2026
Tristian Elyas BDC05180

SITE CALCULATIONS AS PER SEPP

TOTAL SITE AREA :	790.3 SQM
MAX. FLOOR SPACE AREA ALLOWED:	497.575 SQM
PROPOSED GROUND FLOOR FLOOR SPACE AREA	177.4 SQM
PROPOSED FIRST FLOOR FLOOR SPACE AREA	194.9 SQM
PROPOSED FLOOR SPACE AREA :	372.3 SQM
MIN LANDSCAPING AREA REQUIRED:	290.15 SQM
PROPOSED FRONT LANDSCAPING AREA:	198.2 SQM
PROPOSED REAR LANDSCAPING AREA:	149.8 SQM
PROPOSED LANDSCAPED AREA:	348 SQM
MIN PRIVATE OPEN SPACE REQUIRED	16 SQM
PROPOSED PRIVATE OPEN SPACE	16 SQM
ARTICULATION AREA - 25% = 15.8 SQM	63.2 SQM
UTILISED ARTICULATION AREA 24.84%	15.7 SQM

SITE CALCULATION

1 : 50

SLEIMAN
PROPERTY GROUP

bdaa
ACCREDITED
BUILDING DESIGNER

BDAA Reg No. 6973

NOTE
Do not scale drawing, figured dimension only to be used.
All measurements are in millimetres.

COPYRIGHT
All rights reserved.
These drawings, plans and specifications and the copyright are the property of SLEIMAN PROPERTY GROUP and must not be used, reproduced or copied wholly or in part without the written permission of SLEIMAN PROPERTY GROUP

Northpoint



NO.	DRAWING:	BY:	DATE:	AMENDMENTS:
1	ISSUE FOR REVIEW		17/02/26	
2	ISSUE FOR CDC		13/04/26	
3				
4				
5				
6				
7				

CLIENT: **DEBRA FRANCIS**

ADDRESS: **42 DARTMOOR CIRCUIT EMU HEIGHTS**

AREAS


Project number 135

Date FEB26

Drawn by LS

A004

SAs indicated

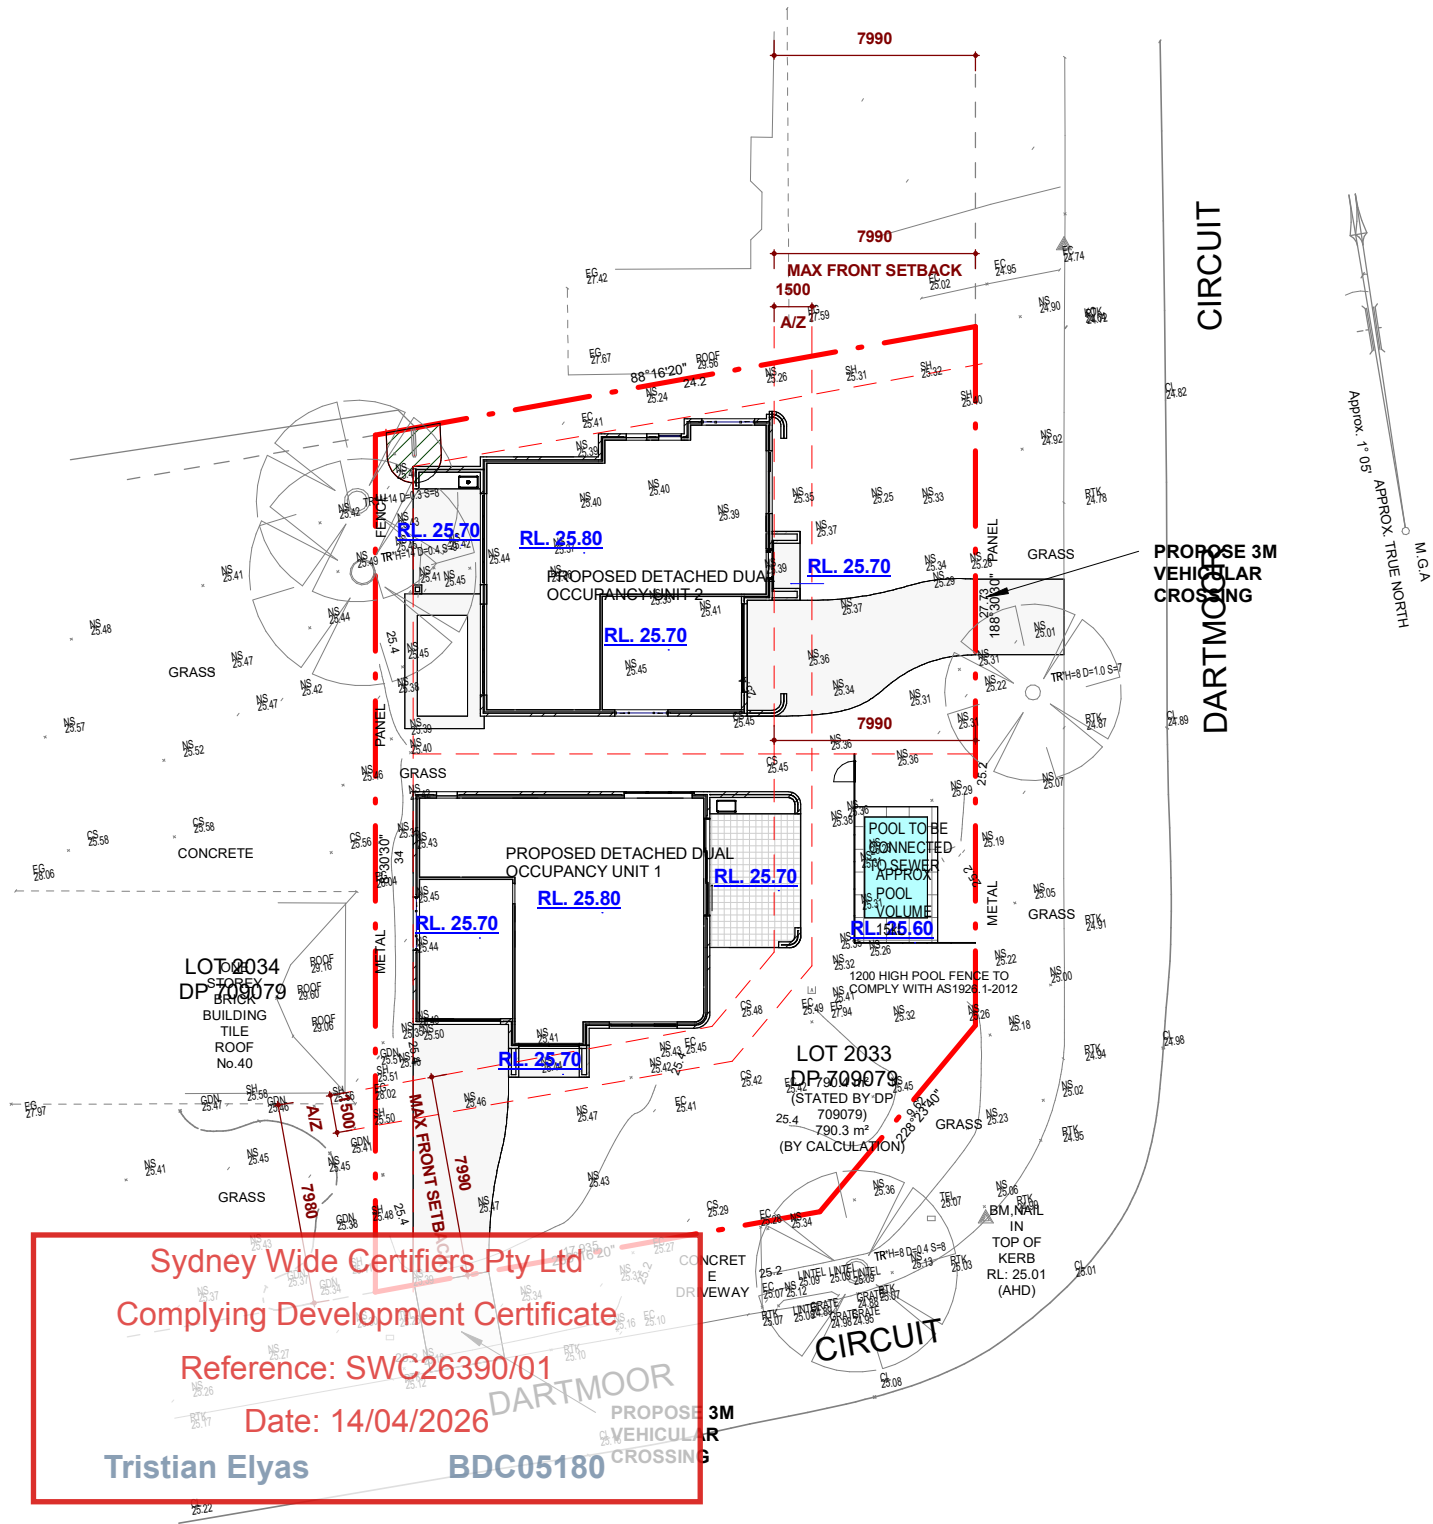

Sydney Wide Certifiers Pty Ltd
Complying Development Certificate
Reference: SWC26390/01
Date: 14/04/2026
Tristian Elyas BDC05180

SITE CONTEXT

1 : 300

SLEIMAN

PROPERTY GROUP

bdaa

ACCREDITED

BUILDING DESIGNER

BDA Reg No. 6973

NOTE

Do not scale drawing, figured dimension only to be used.

All measurements are in millimetres.

COPYRIGHT


All rights reserved.

These drawings, plans and specifications and the copyright are the property of SLEIMAN PROPERTY GROUP and must not be used, reproduced or copied wholly or in part without the written permission of SLEIMAN PROPERTY GROUP

Northpoint

NO.	DRAWING:	BY:	DATE:	AMENDMENTS:
1	ISSUE FOR REVIEW		17/02/26	
2	ISSUE FOR CDC		13/04/26	
3				
4				
5				
6				
7				

CLIENT: DEBRA FRANCIS	SITE CONTEXT	
ADDRESS: 42 DARTMOOR CIRCUIT EMU HEIGHTS	Project number	135
	Date	FEB26
	Drawn by	LS
		A005
		Scale 1 : 300

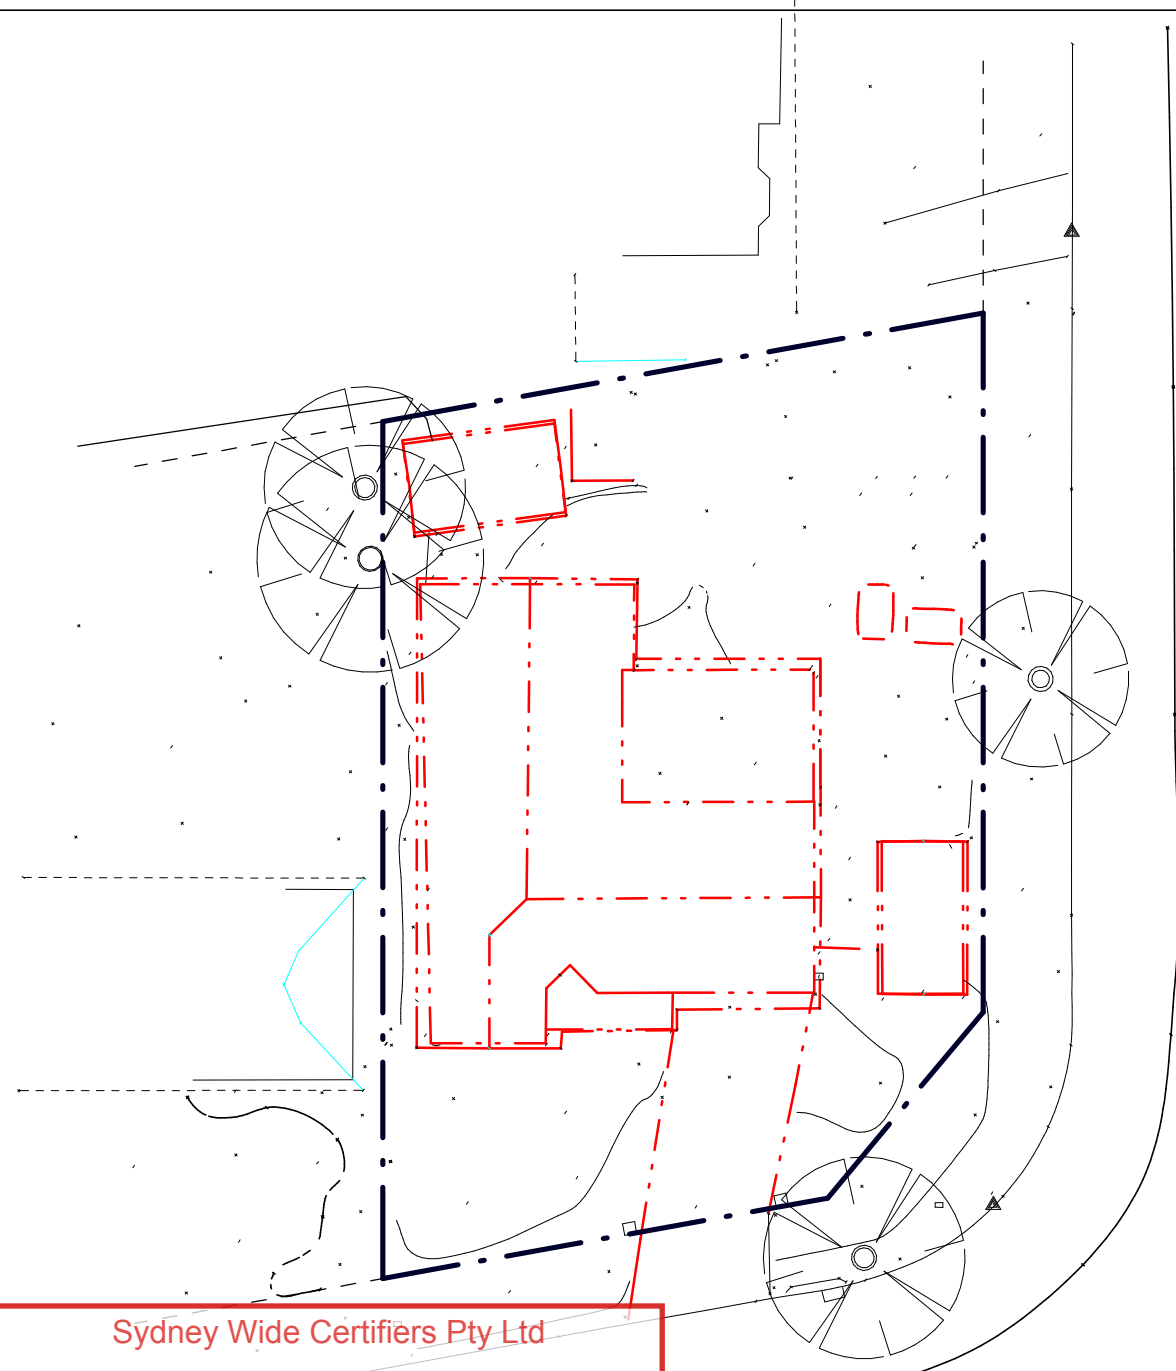


Sydney Wide Certifiers Pty Ltd
Complying Development Certificate
Reference: SWC26390/01
Date: 14/04/2026
Tristian Elyas BDC05180

DEMOLITION PLAN


1 : 300

SEDIMENT CONTROL LEGEND

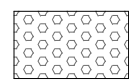- 
- SILT BARRIER FENCE

SITE TOILET

SITE SHED

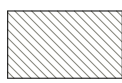STABILIZED SITE ACCESS
- 
- SITE ACCESS


MATERIAL STORAGE

WASTE STORAGE



A FILTER FENCE SHALL BE CONSTRUCTED BY STRETCHING A FLEXIBLE FABRIC (PROPEX OR SIMILAR) BETWEEN POSTS AT 2000mm CENTRES. FABRIC SHALL BE BURIED 150mm ALONG ITS LOWER EDGE. DRAINAGE CHANNELS SHALL LEAD TO A STRAW BALE LOCATED AT THE REAR OF THE SITE.

ALL VEHICLES TO HAVE WHEELS WASHED DOWN PRIOR TO LEAVING THE SITE.

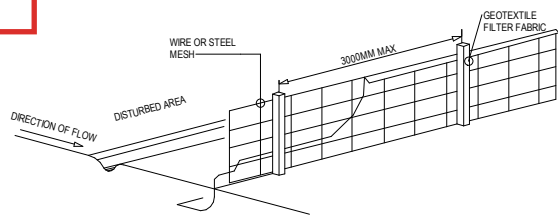

SEDIMENT FENCE - N.T.S

 DENOTES ITEMS TO BE DEMOLISHED

DEMOLITION TO COMPLY WITH AS 2601-2001 : THE DEMOLITION OF STRUCTURES
SERVICES TO BE DISCONNECTED PRIOR TO DEMOLITION
DEMOLITION TO COMMENCE UPON NOTIFICATION OF APPOINTED CERTIFYING AUTHORITY

SLEIMAN
PROPERTY GROUP


ACCREDITED
BUILDING DESIGNER
BDAA Reg No. 6973

NOTE
Do not scale drawing, figured dimension only to be used.
All measurements are in millimetres.

COPYRIGHT
All rights reserved.
These drawings, plans and specifications and the copyright are the property of SLEIMAN PROPERTY GROUP and must not be used, reproduced or copied wholly or in part without the written permission of SLEIMAN PROPERTY GROUP

Northpoint




NO.	DRAWING:	BY:	DATE:	AMENDMENTS:
1	ISSUE FOR REVIEW		17/02/26	
2	ISSUE FOR CDC		13/04/26	
3				
4				
5				
6				
7				

CLIENT: DEBRA FRANCIS

ADDRESS: 42 DARTMOOR CIRCUIT EMU HEIGHTS

DEMOLITION PLAN

Project number	135	A050 SAs indicated
Date	FEB26	
Drawn by	LS	

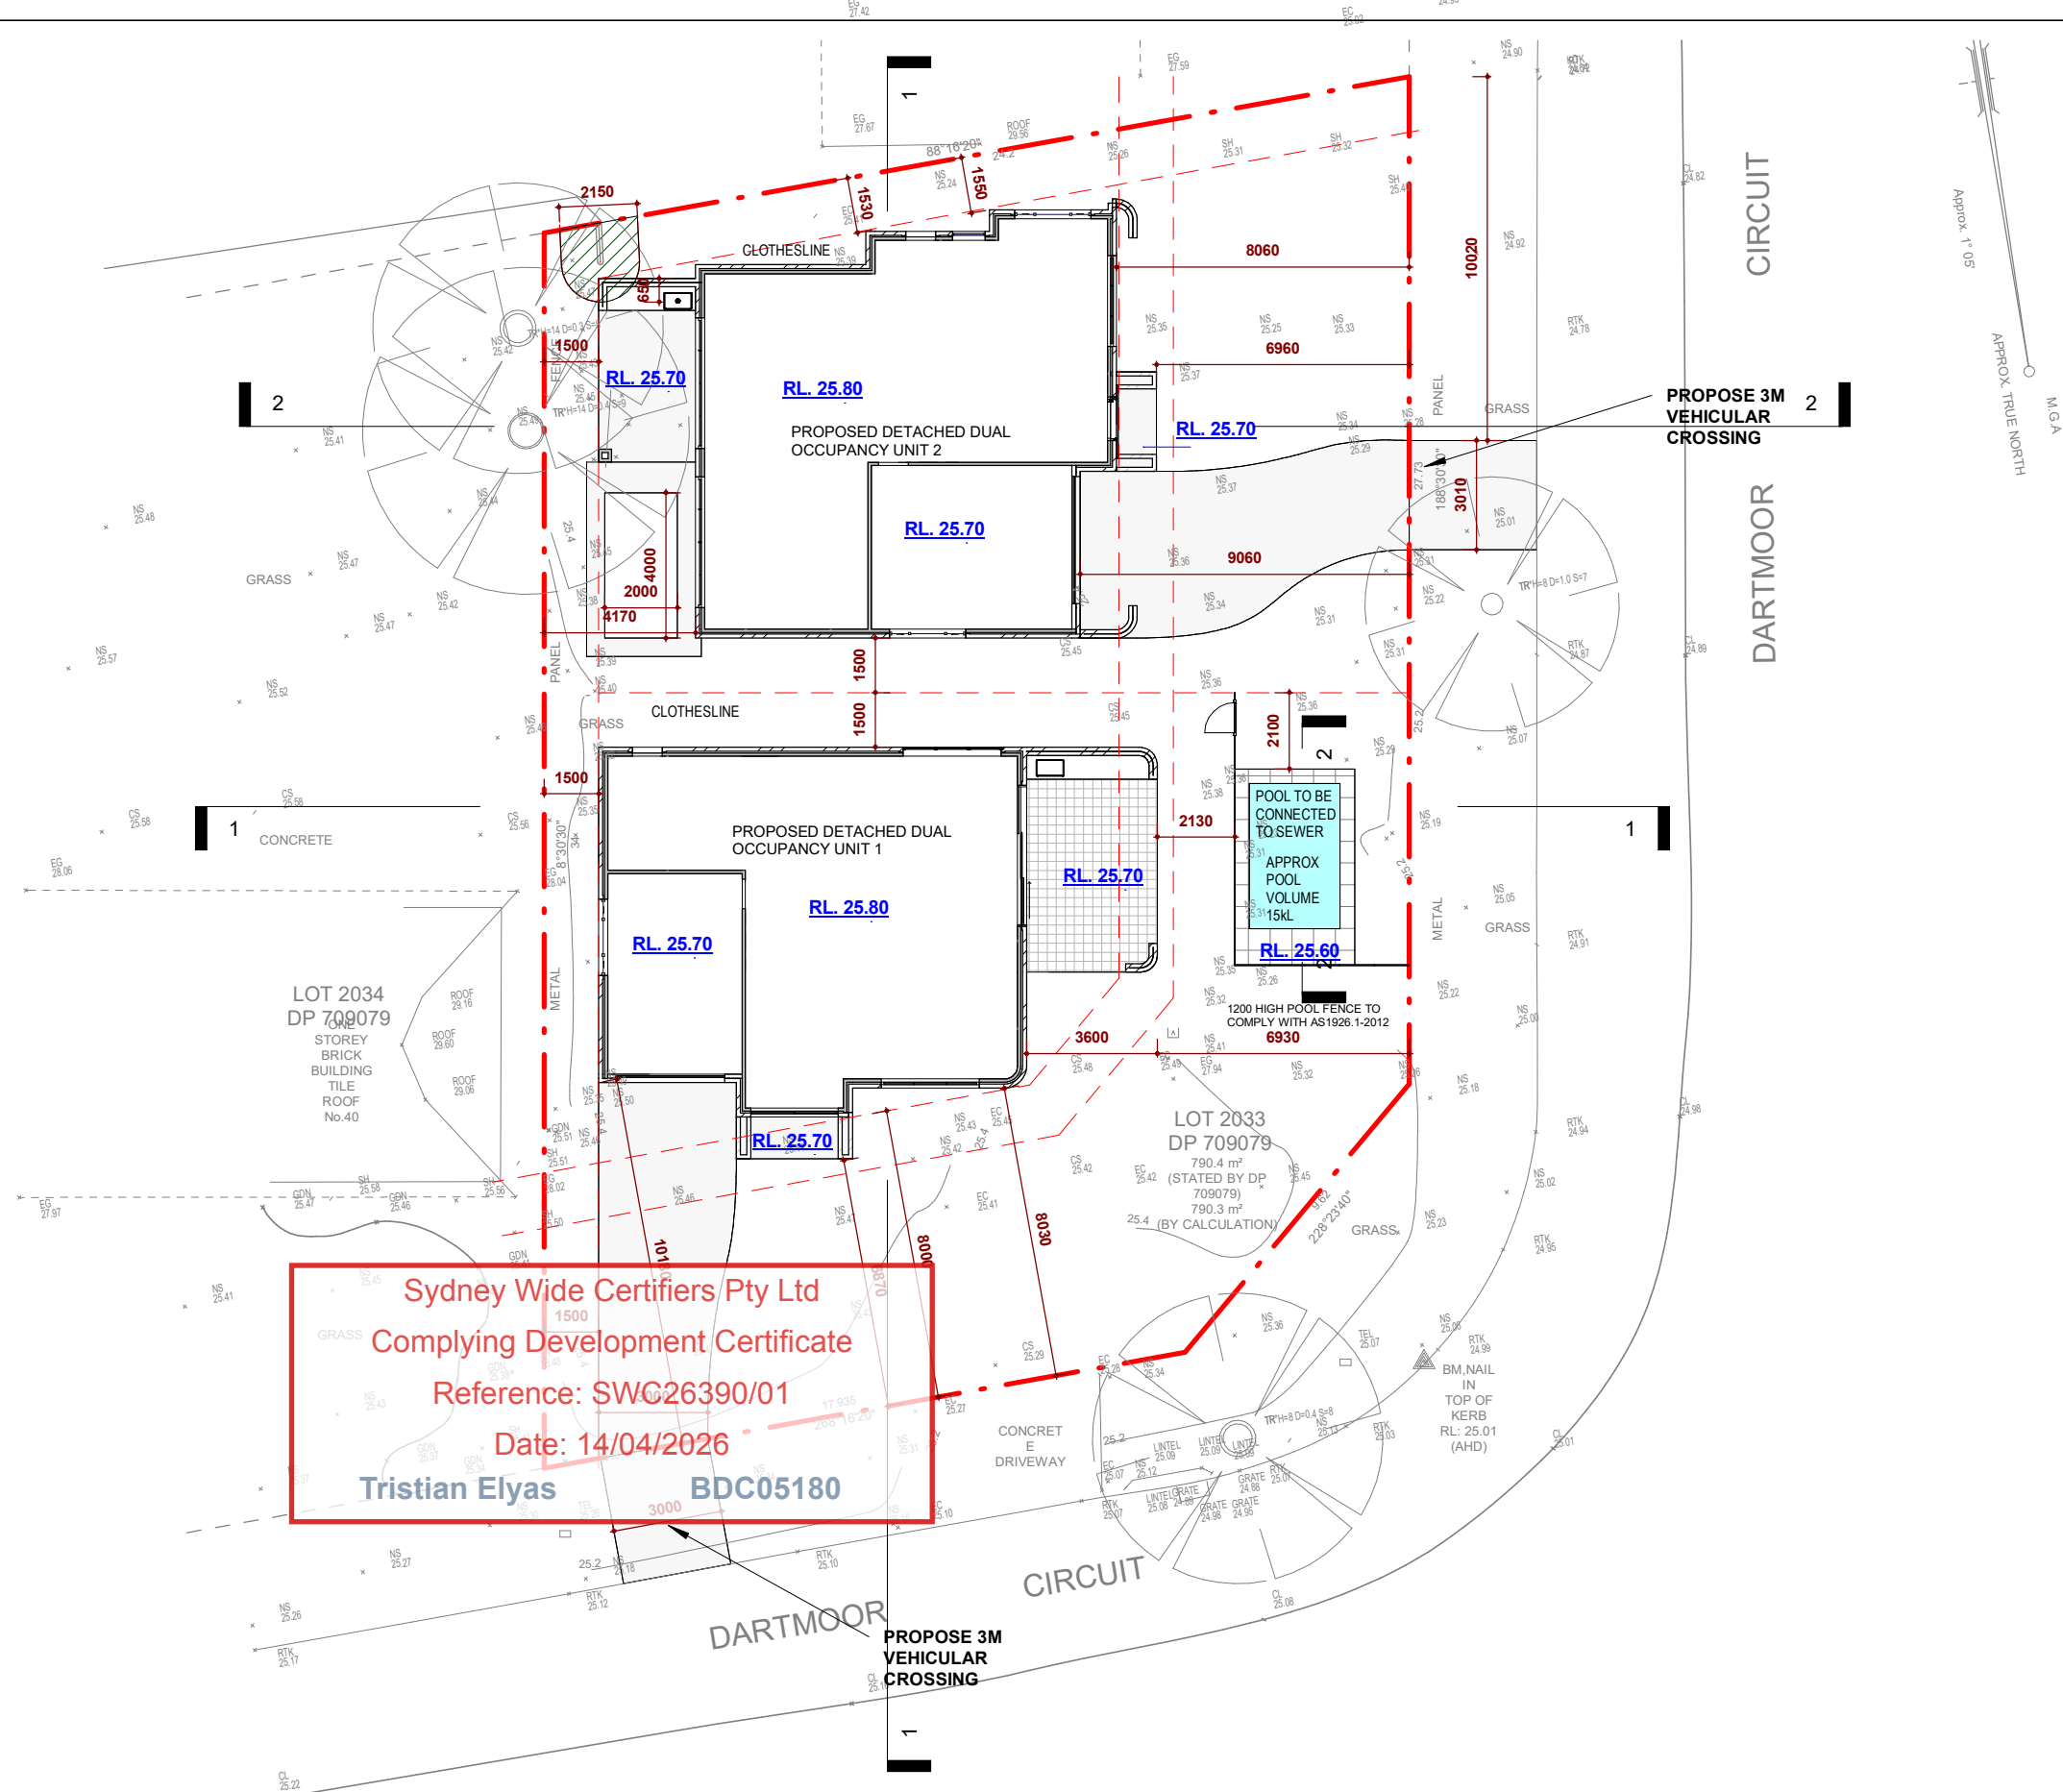

SITE/GROUND FLOOR

1 : 200

SLEIMAN
PROPERTY GROUP

bdaa
ACCREDITED
BUILDING DESIGNER

BDAA Reg No. 6973

NOTE
Do not scale drawing, figured dimension only to be used.
All measurements are in millimetres.

COPYRIGHT
All rights reserved.
These drawings, plans and specifications and the copyright are the property of SLEIMAN PROPERTY GROUP and must not be used, reproduced or copied wholly or in part without the written permission of SLEIMAN PROPERTY GROUP

Northpoint



NO.	DRAWING:	BY:	DATE:	AMENDMENTS:
1	ISSUE FOR REVIEW		17/02/26	
2	ISSUE FOR CDC		13/04/26	
3				
4				
5				
6				
7				

CLIENT: **DEBRA FRANCIS**

ADDRESS: **42 DARTMOOR CIRCUIT EMU HEIGHTS**

SITE/GROUND FLOOR
PLAN


Project number 135

Date FEB26

Drawn by LS

A101

Scale 1 : 200

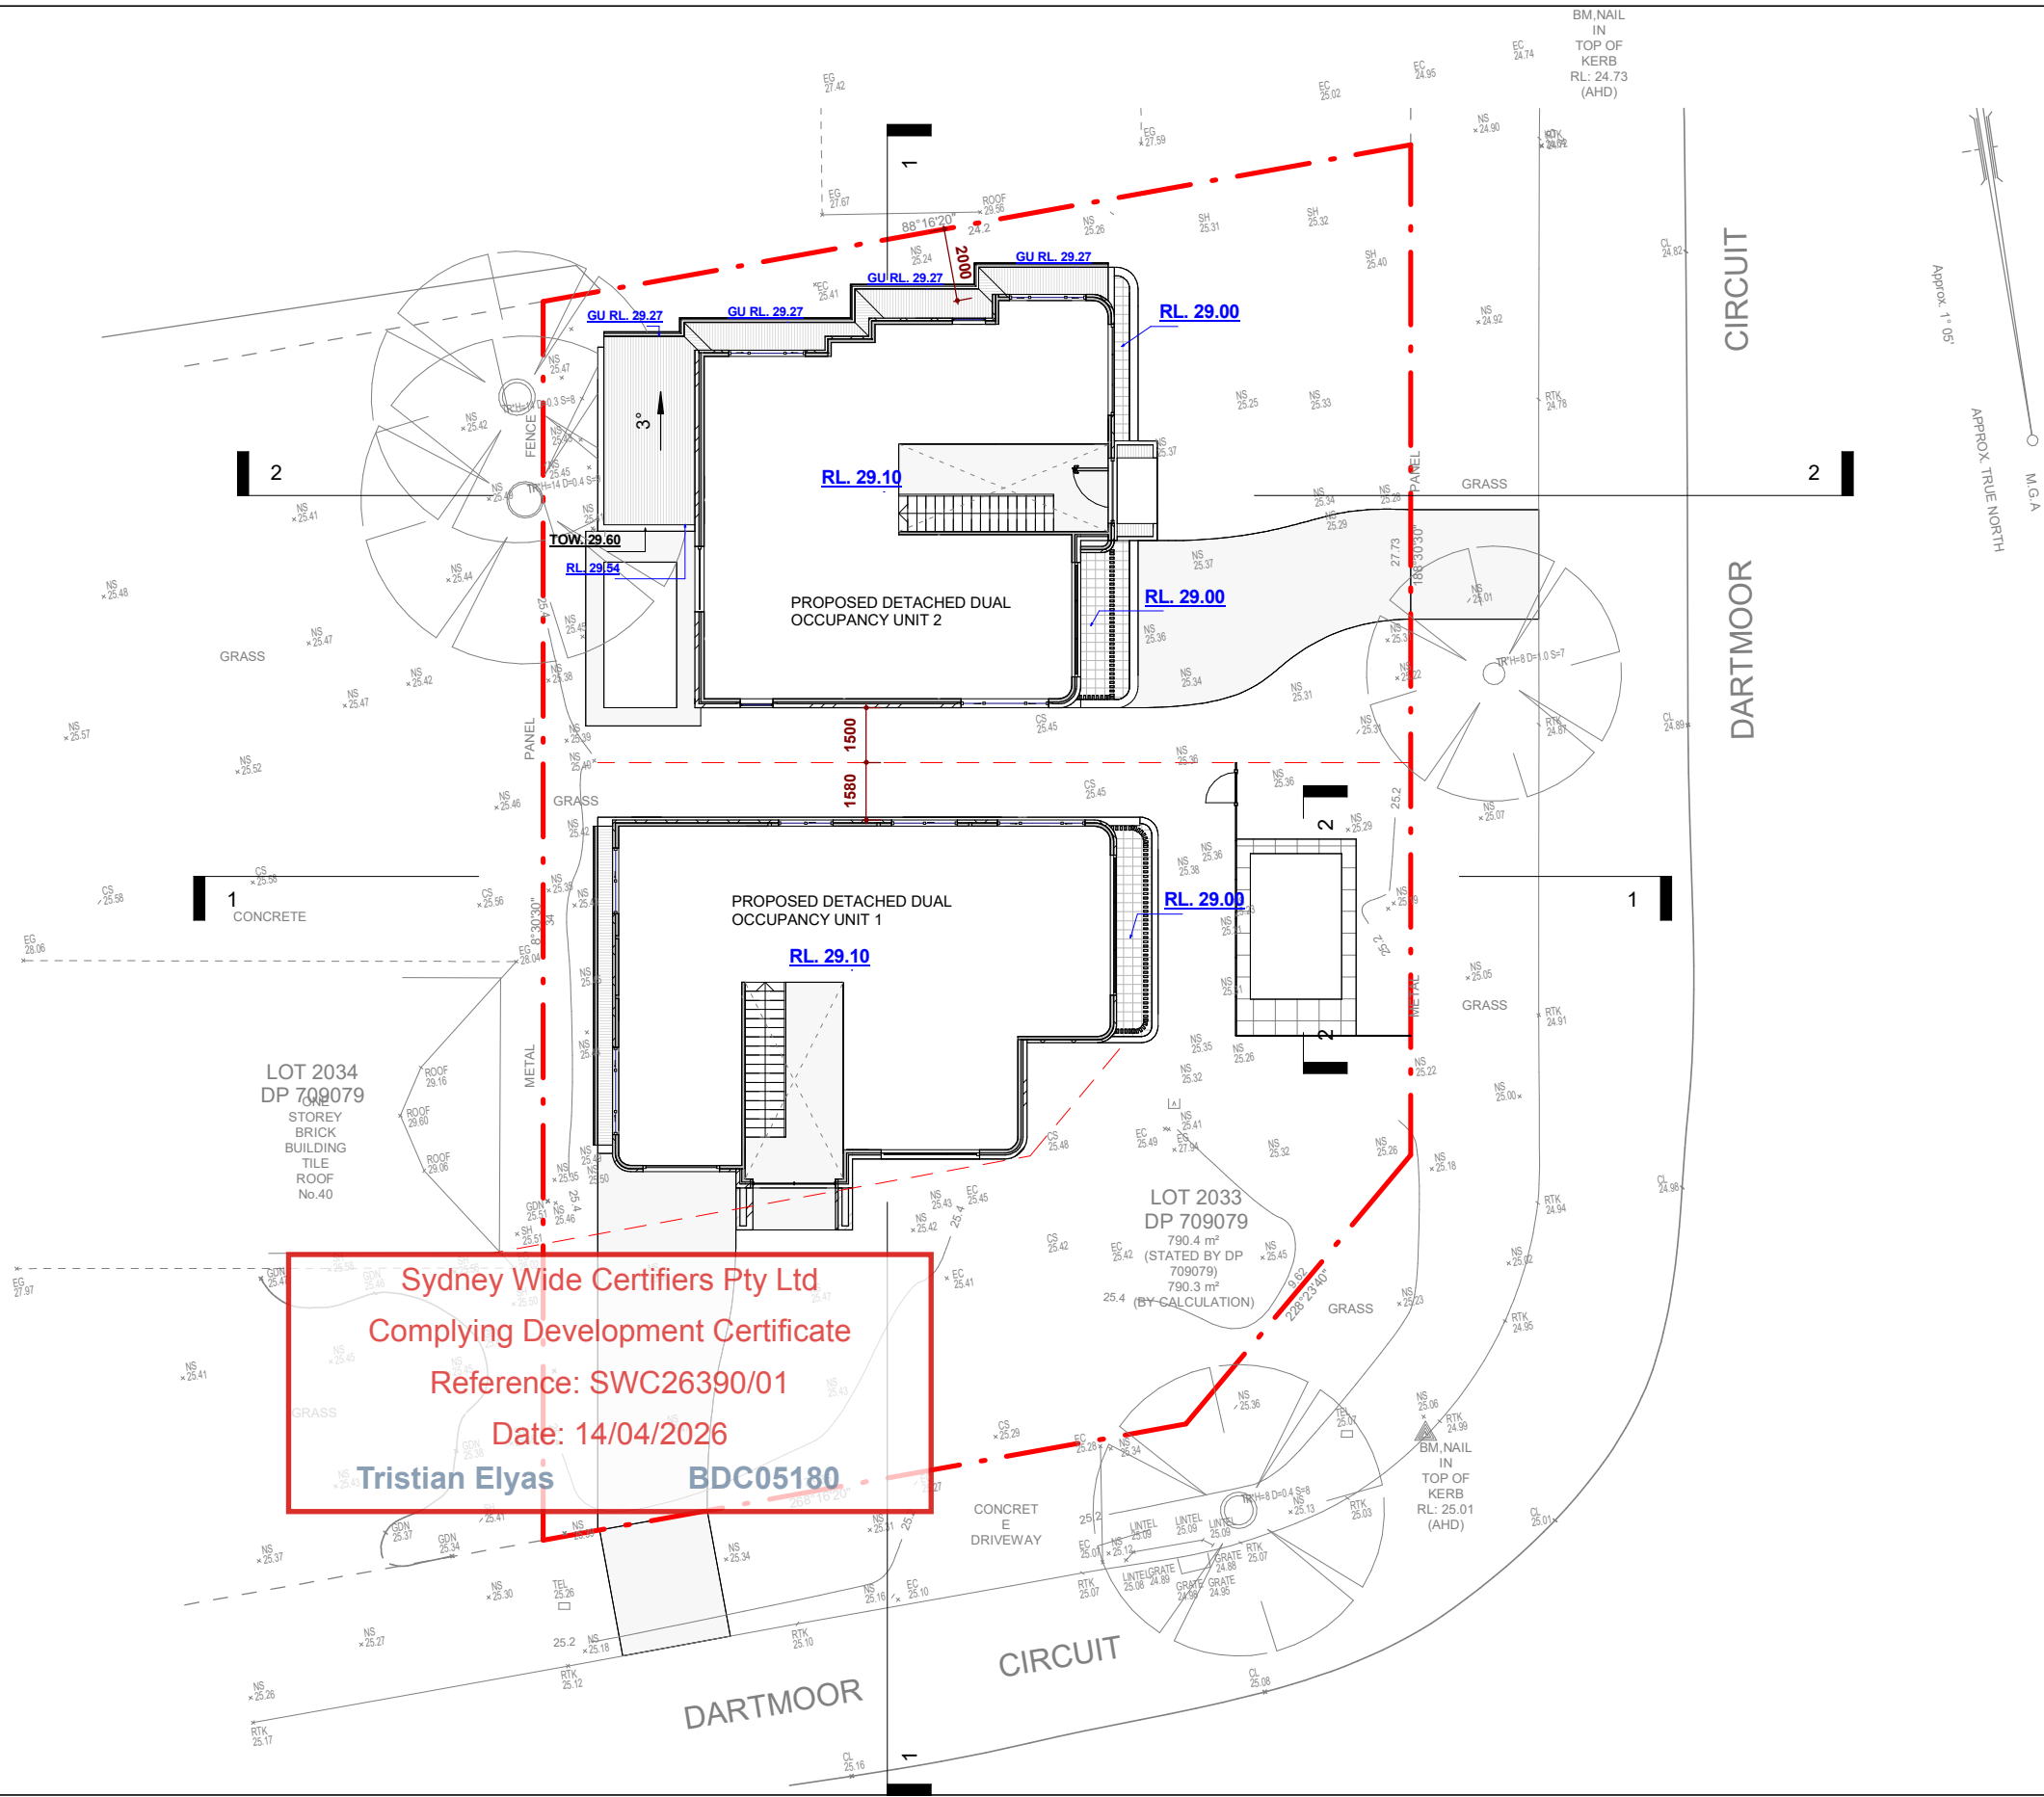

SITE/FIRST FLOOR

1 : 200

SLEIMAN

PROPERTY GROUP

bdaa

ACCREDITED

BUILDING DESIGNER

BDA Reg No. 6973


NOTE
Do not scale drawing, figured dimension only to be used.
All measurements are in millimetres.

COPYRIGHT
All rights reserved.
These drawings, plans and specifications and the copyright are the property of SLEIMAN PROPERTY GROUP and must not be used, reproduced or copied wholly or in part without the written permission of SLEIMAN PROPERTY GROUP



NO.	DRAWING:	BY:	DATE:	AMENDMENTS:
1	ISSUE FOR REVIEW		17/02/26	
2	ISSUE FOR CDC		13/04/26	
3				
4				
5				
6				
7				

CLIENT: DEBRA FRANCIS		SITE/FIRST FLOOR PLAN	
ADDRESS: 42 DARTMOOR CIRCUIT EMU HEIGHTS		Project number	135
		Date	FEB26
		Drawn by	LS
		A102	
		Scale 1 : 200	

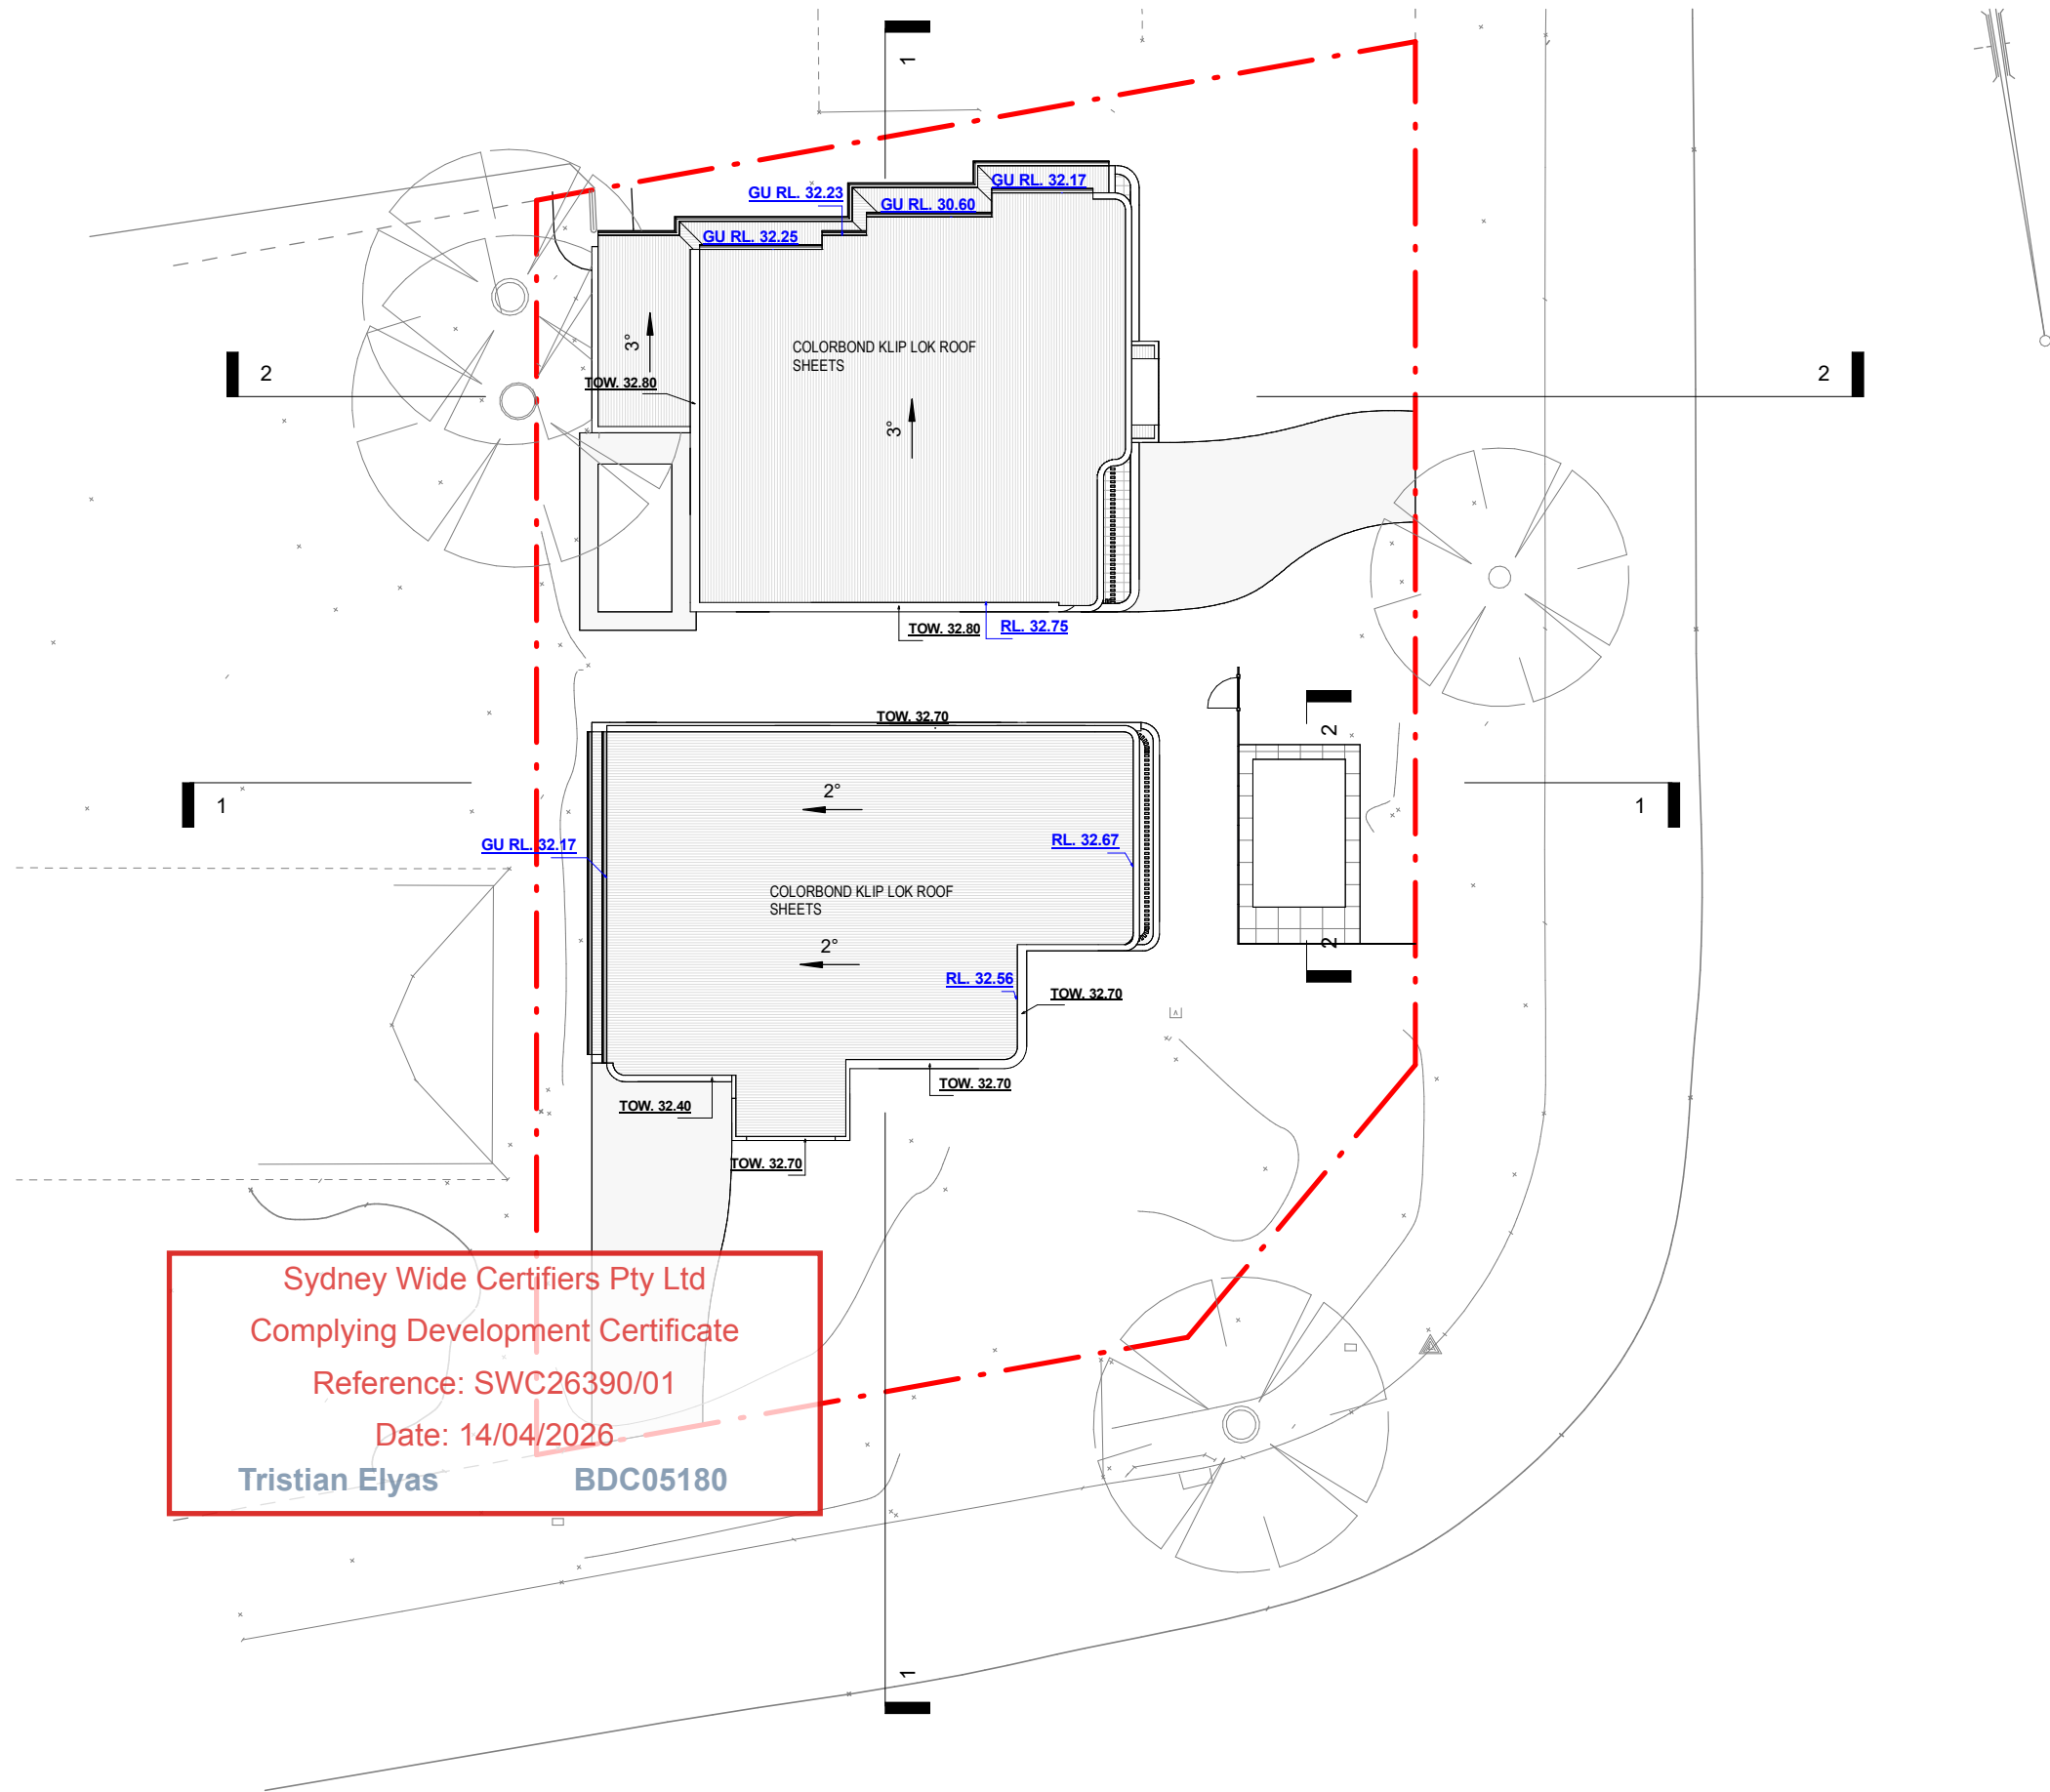

SITE/ROOF PLAN

1 : 200

SLEIMAN

PROPERTY GROUP

bdaa

ACCREDITED

BUILDING DESIGNER

BDAA Reg No. 6973

NOTE

Do not scale drawing, figured dimension only to be used.

All measurements are in millimetres.

COPYRIGHT


All rights reserved.

These drawings, plans and specifications and the copyright are the property of SLEIMAN PROPERTY GROUP and must not be used, reproduced or copied wholly or in part without the written permission of SLEIMAN PROPERTY GROUP

Northpoint

NO.	DRAWING:	BY:	DATE:	AMENDMENTS:
1	ISSUE FOR REVIEW		17/02/26	
2	ISSUE FOR CDC		13/04/26	
3				
4				
5				
6				
7				

CLIENT: DEBRA FRANCIS	SITE/ROOF PLAN	
ADDRESS: 42 DARTMOOR CIRCUIT EMU HEIGHTS	Project number	135
	Date	FEB26
	Drawn by	LS
		A103
		Scale 1 : 200

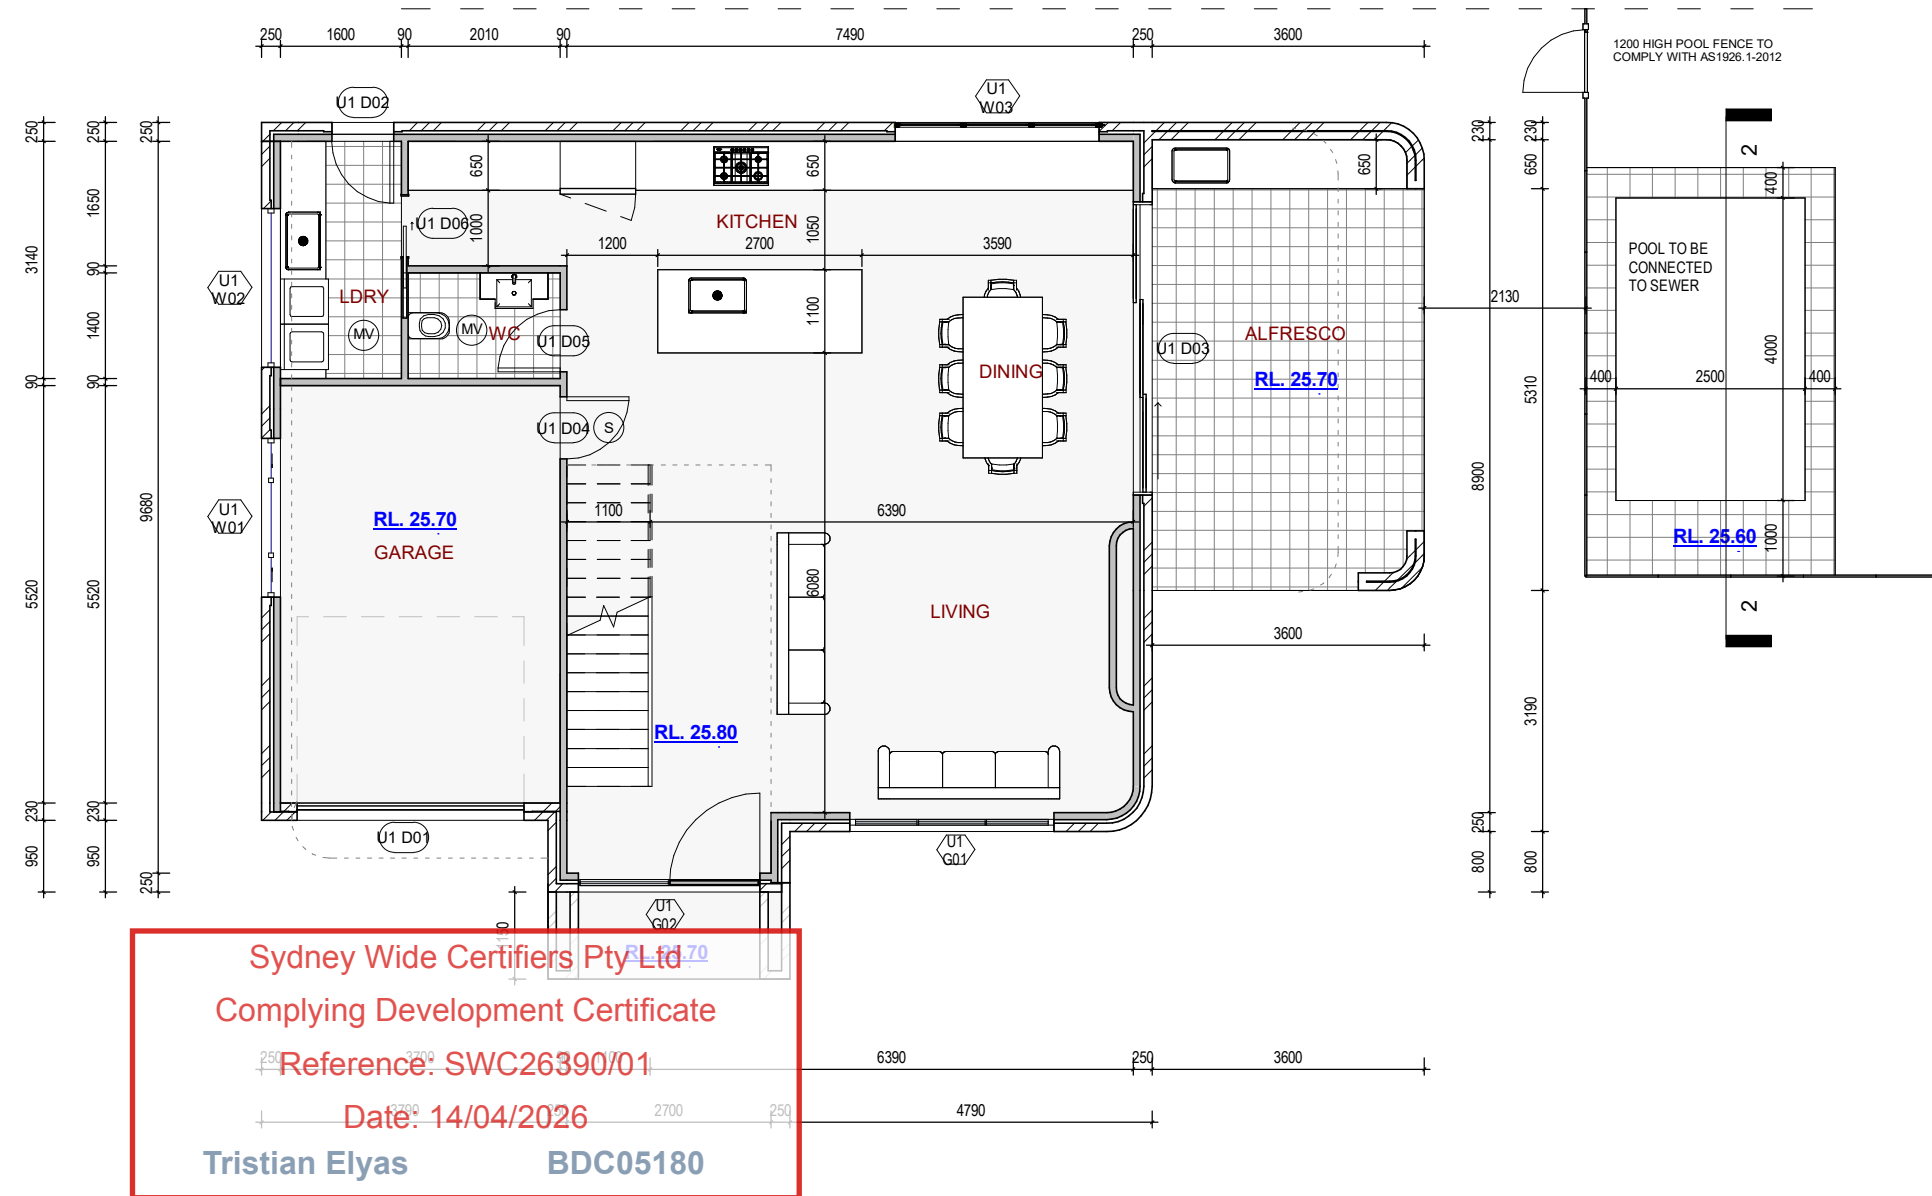

U1 GROUND FLOOR

1 : 100

SLEIMAN
PROPERTY GROUP

bdaa
ACCREDITED
BUILDING DESIGNER

BDAA Reg No. 6973

NOTE
Do not scale drawing, figured dimension only to be used.
All measurements are in millimetres.

COPYRIGHT
All rights reserved.
These drawings, plans and specifications and the copyright are the property
of SLEIMAN PROPERTY GROUP and must not be used, reproduced or
copied wholly or in part without the written permission of SLEIMAN
PROPERTY GROUP

Northpoint



NO.	DRAWING:	BY:	DATE:	AMENDMENTS:
1	ISSUE FOR REVIEW		17/02/26	
2	ISSUE FOR CDC		13/04/26	
3				
4				
5				
6				
7				

CLIENT: **DEBRA FRANCIS**

ADDRESS: **42 DARTMOOR CIRCUIT EMU
HEIGHTS**

GROUND FLOOR PLAN


Project number 135

Date FEB26

Drawn by LS

A201

Scale 1 : 100

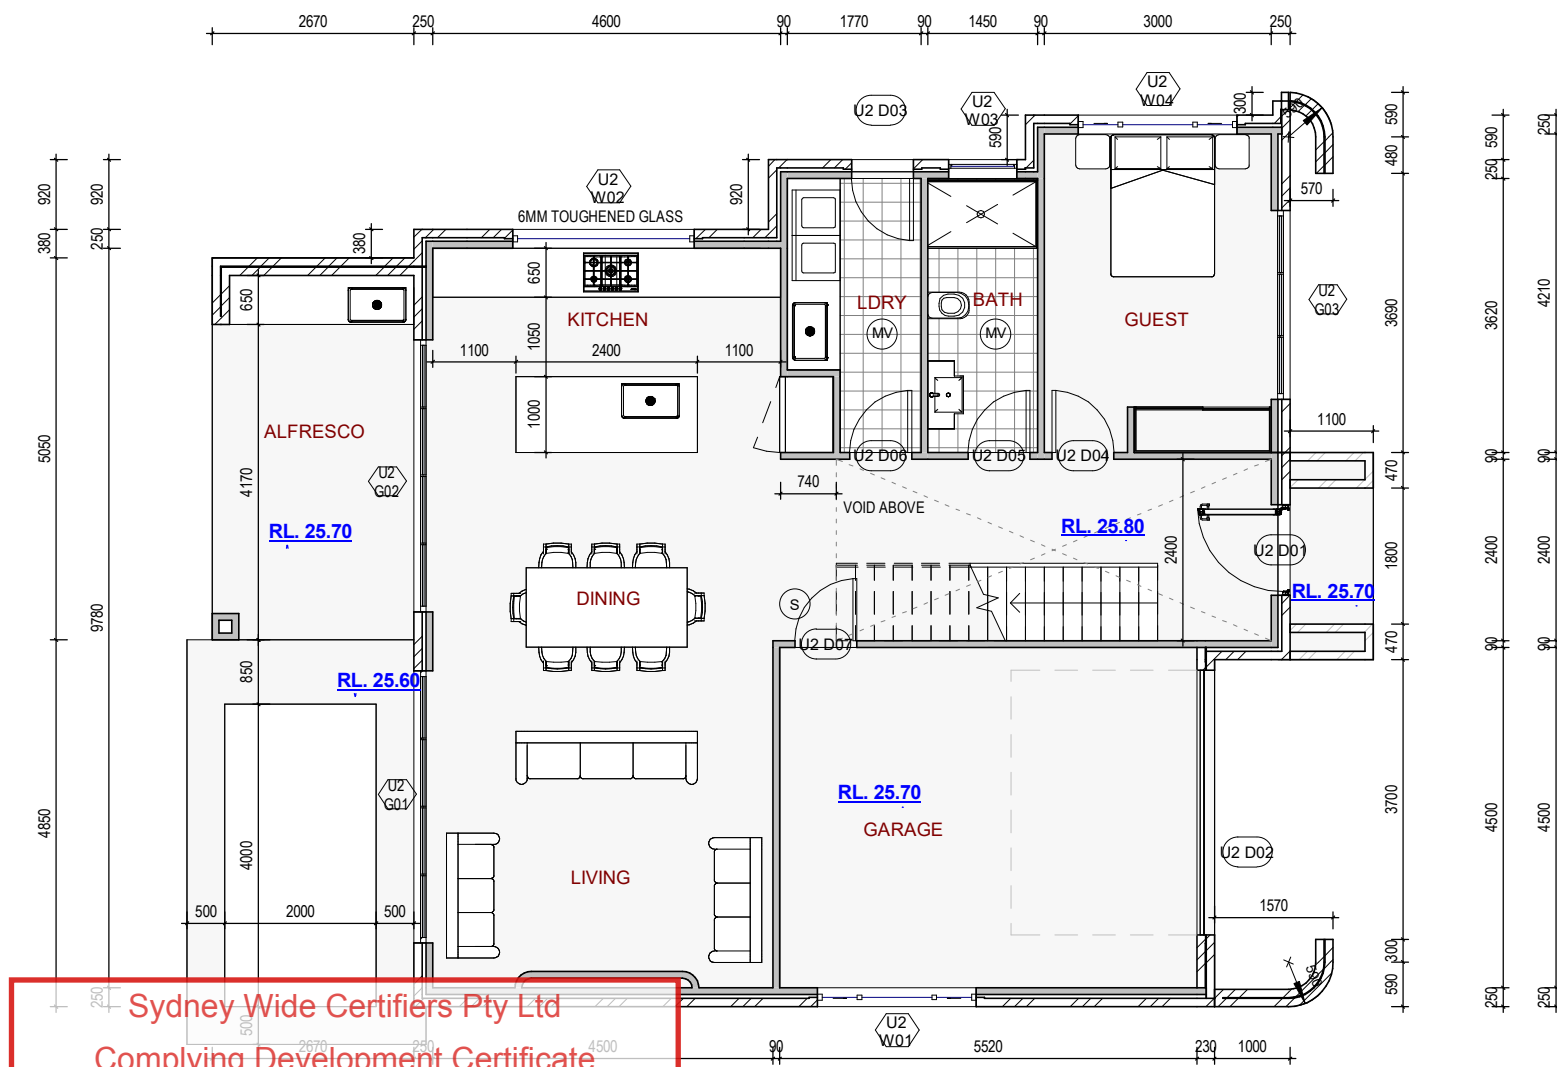

Sydney Wide Certifiers Pty Ltd
Complying Development Certificate
Reference: SWC26390/01
Date: 14/04/2026
Tristian Elyas BDC05180

U2 GROUND FLOOR

1 : 100

SLEIMAN

PROPERTY GROUP

bdaa

ACCREDITED

BUILDING DESIGNER

BDAA Reg No. 6973

NOTE

Do not scale drawing, figured dimension only to be used.
All measurements are in millimetres.


COPYRIGHT

All rights reserved.
These drawings, plans and specifications and the copyright are the property
of SLEIMAN PROPERTY GROUP and must not be used, reproduced or
copied wholly or in part without the written permission of SLEIMAN
PROPERTY GROUP

Northpoint

NO.	DRAWING:	BY:	DATE:	AMENDMENTS:
1	ISSUE FOR REVIEW		17/02/26	
2	ISSUE FOR CDC		13/04/26	
3				
4				
5				
6				
7				

CLIENT: DEBRA FRANCIS	U2 GROUND FLOOR PLAN	
	Project number	135
	Date	FEB26
	Drawn by	LS
ADDRESS: 42 DARTMOOR CIRCUIT EMU HEIGHTS		A202
		Scale 1 : 100

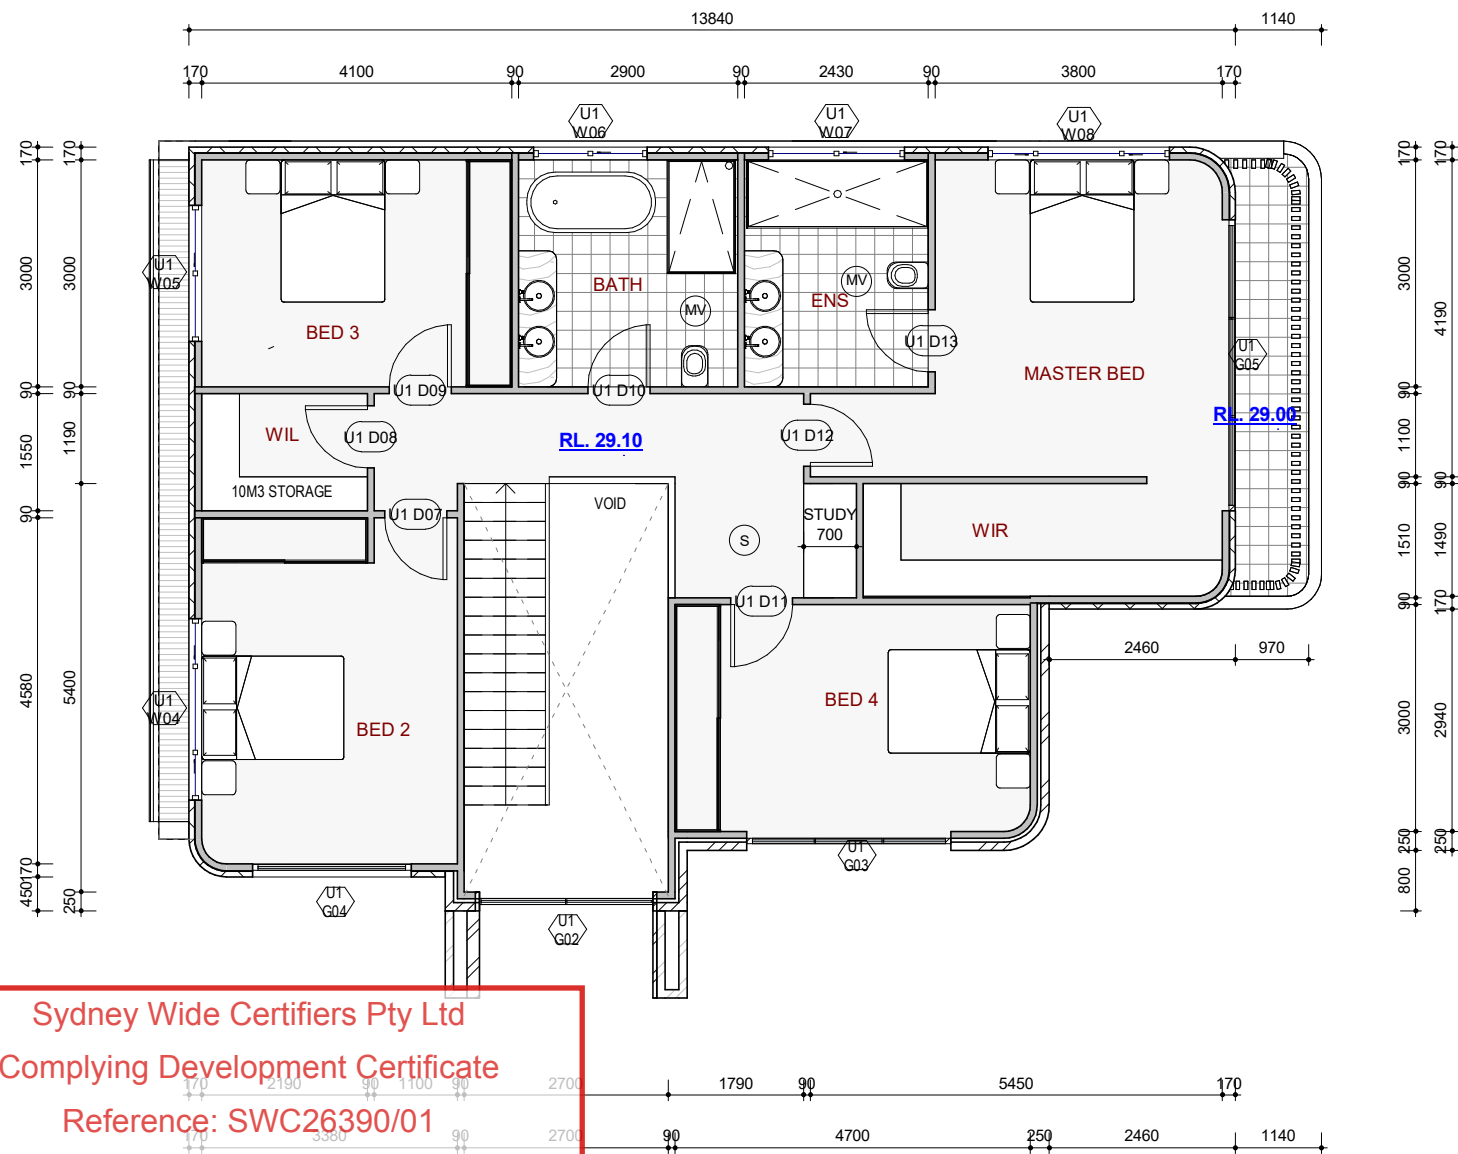

U1 FIRST FLOOR PLAN

1 : 100

SLEIMAN
PROPERTY GROUP

bdaa
ACCREDITED
BUILDING DESIGNER

BDAA Reg No. 6973

NOTE
Do not scale drawing, figured dimension only to be used.
All measurements are in millimetres.

COPYRIGHT
All rights reserved.
These drawings, plans and specifications and the copyright are the property
of SLEIMAN PROPERTY GROUP and must not be used, reproduced or
copied wholly or in part without the written permission of SLEIMAN
PROPERTY GROUP

Northpoint



NO.	DRAWING:	BY:	DATE:	AMENDMENTS:
1	ISSUE FOR REVIEW		17/02/26	
2	ISSUE FOR CDC		13/04/26	
3				
4				
5				
6				
7				

CLIENT: **DEBRA FRANCIS**

ADDRESS: **42 DARTMOOR CIRCUIT EMU
HEIGHTS**

U1 FIRST FLOOR PLAN


Project number 135

Date FEB26

Drawn by LS

A203

Scale 1 : 100

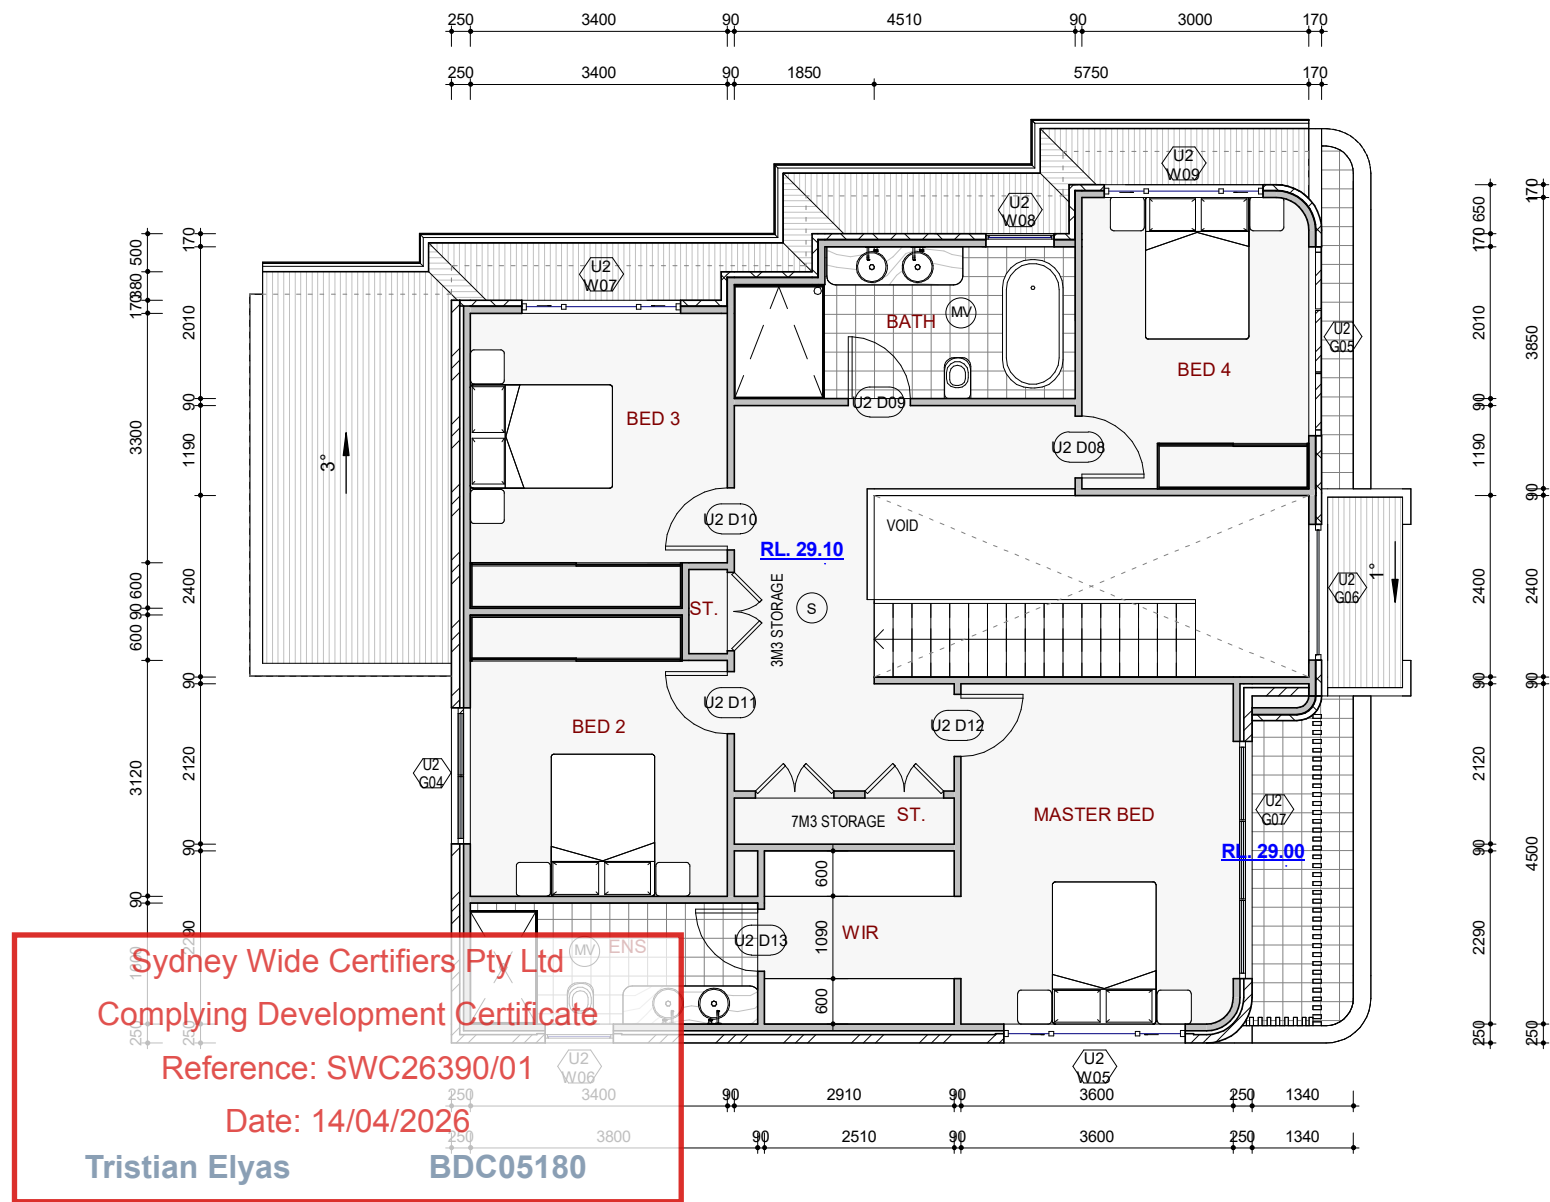

U2 FIRST FLOOR

1 : 100

SLEIMAN

PROPERTY GROUP

bdaa

ACCREDITED

BUILDING DESIGNER

BDAA Reg No. 6973

NOTE

Do not scale drawing, figured dimension only to be used.

All measurements are in millimetres.

COPYRIGHT


All rights reserved.

These drawings, plans and specifications and the copyright are the property of SLEIMAN PROPERTY GROUP and must not be used, reproduced or copied wholly or in part without the written permission of SLEIMAN PROPERTY GROUP

Northpoint


NO.	DRAWING:	BY:	DATE:	AMENDMENTS:
1	ISSUE FOR REVIEW		17/02/26	
2	ISSUE FOR CDC		13/04/26	
3				
4				
5				
6				
7				

CLIENT: DEBRA FRANCIS	U2 FIRST FLOOR PLAN	
ADDRESS: 42 DARTMOOR CIRCUIT EMU HEIGHTS	Project number	135
	Date	FEB26
	Drawn by	LS
		A204
		Scale 1 : 100

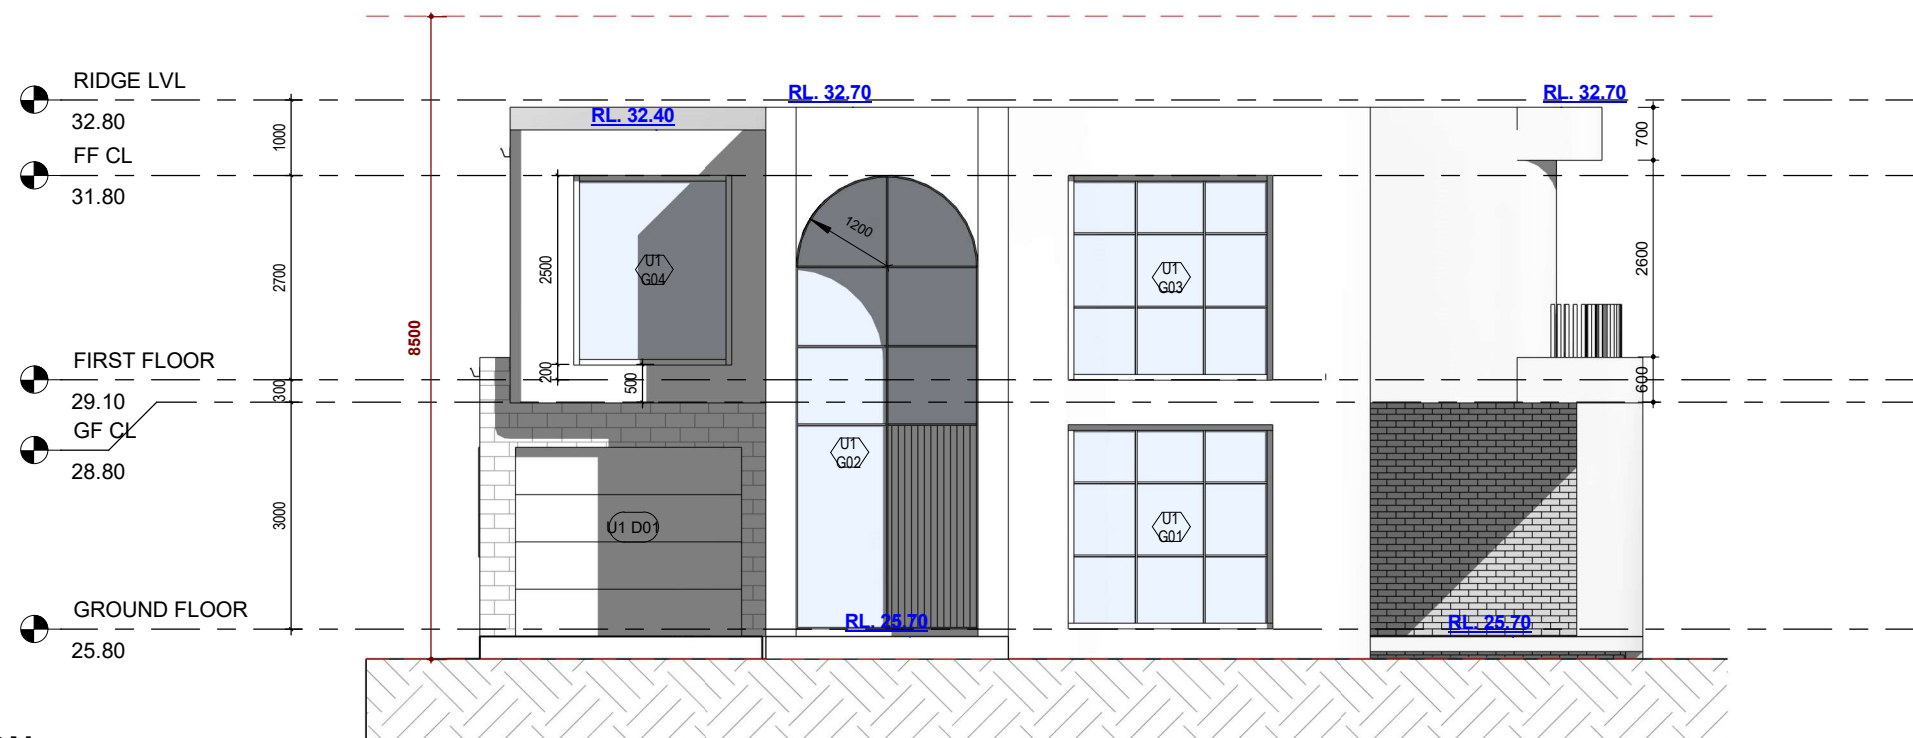

U1 SOUTH ELEVATION

1 : 100

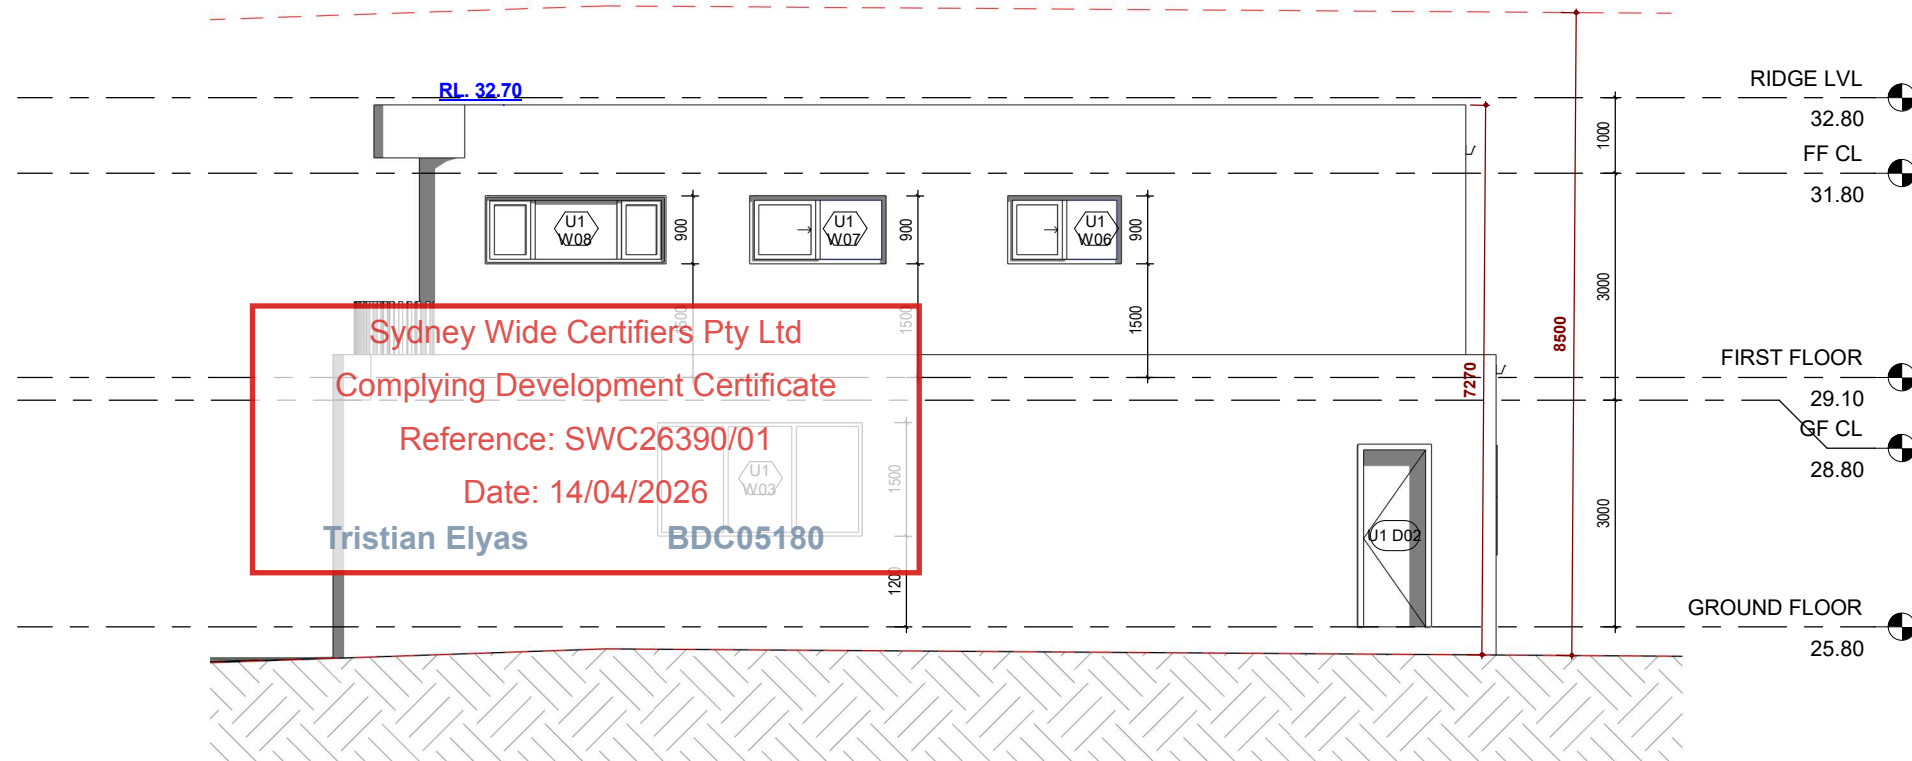

U1 NORTH ELEVATION

1 : 100

SLEIMAN
PROPERTY GROUP

bdaa
ACCREDITED
BUILDING DESIGNER

BDAA Reg No. 6973

NOTE
Do not scale drawing, figured dimension only to be used.
All measurements are in millimetres.

COPYRIGHT
All rights reserved.
These drawings, plans and specifications and the copyright are the property
of SLEIMAN PROPERTY GROUP and must not be used, reproduced or
copied wholly or in part without the written permission of SLEIMAN
PROPERTY GROUP

Northpoint



NO.	DRAWING:	BY:	DATE:	AMENDMENTS:
1	ISSUE FOR REVIEW		17/02/26	
2	ISSUE FOR CDC		13/04/26	
3				
4				
5				
6				
7				

CLIENT: DEBRA FRANCIS

ADDRESS: 42 DARTMOOR CIRCUIT EMU
HEIGHTS

ELEVATIONS


Project number 135

Date FEB26

Drawn by LS


A301

Scale 1 : 100

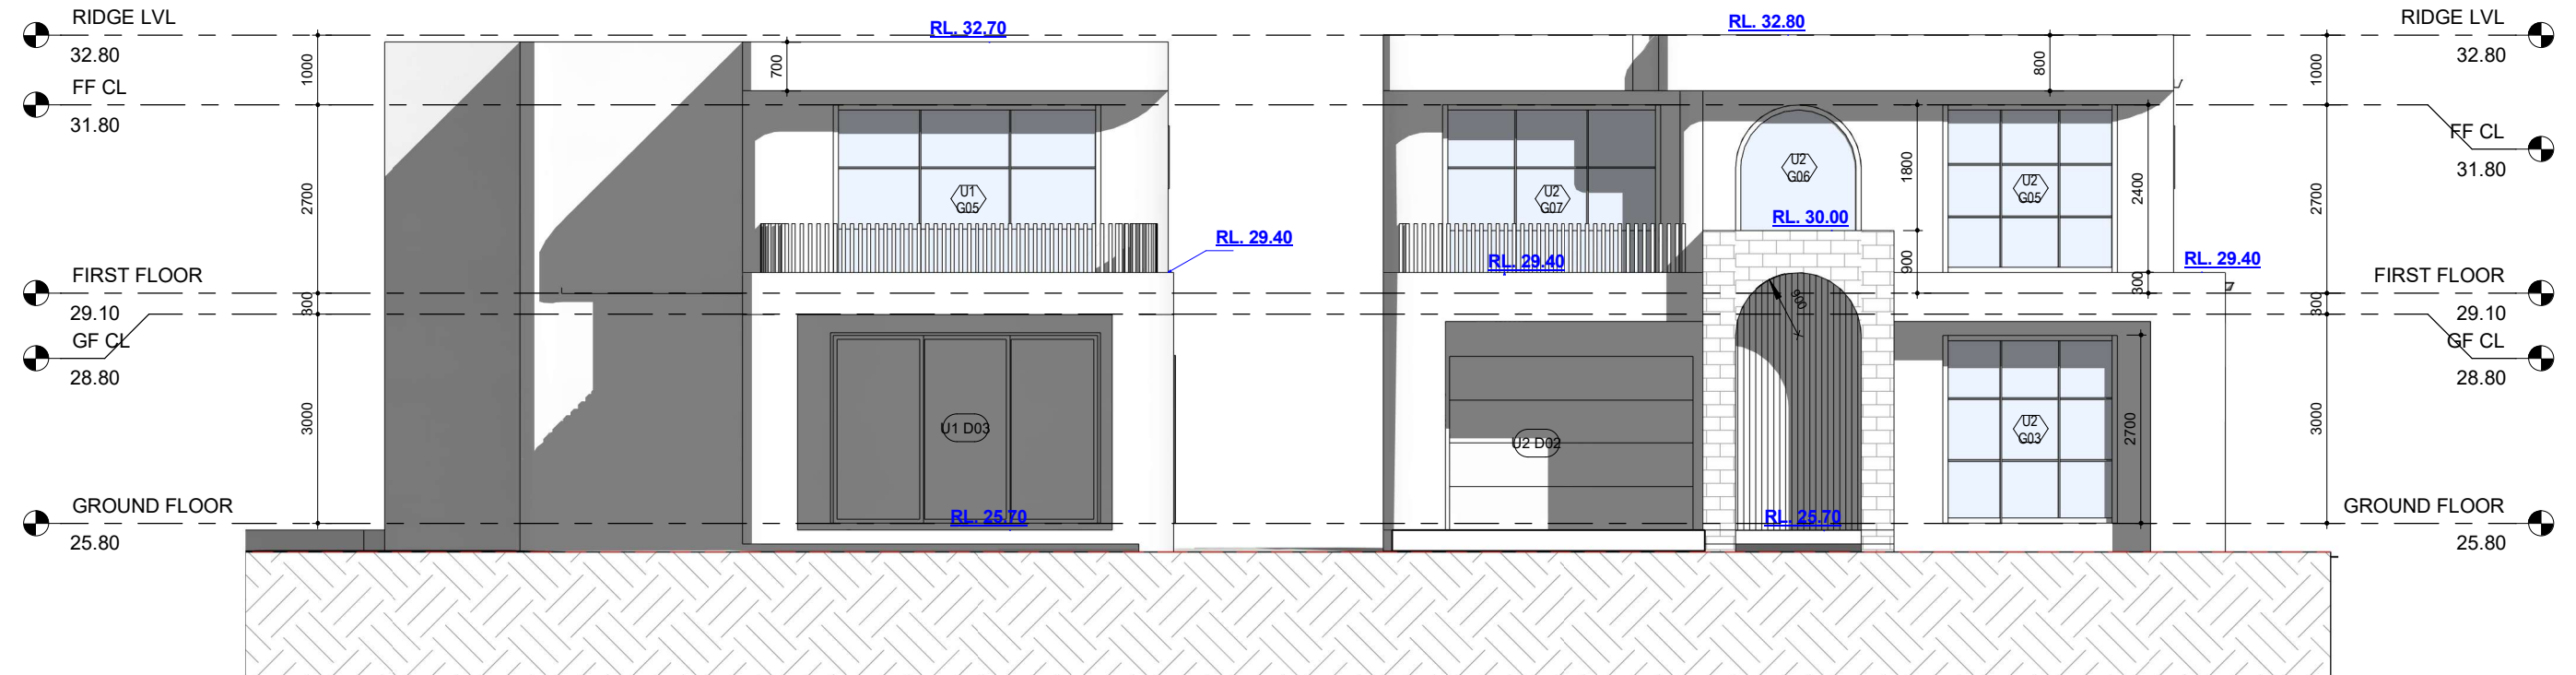

EAST ELEVATION

1 : 100

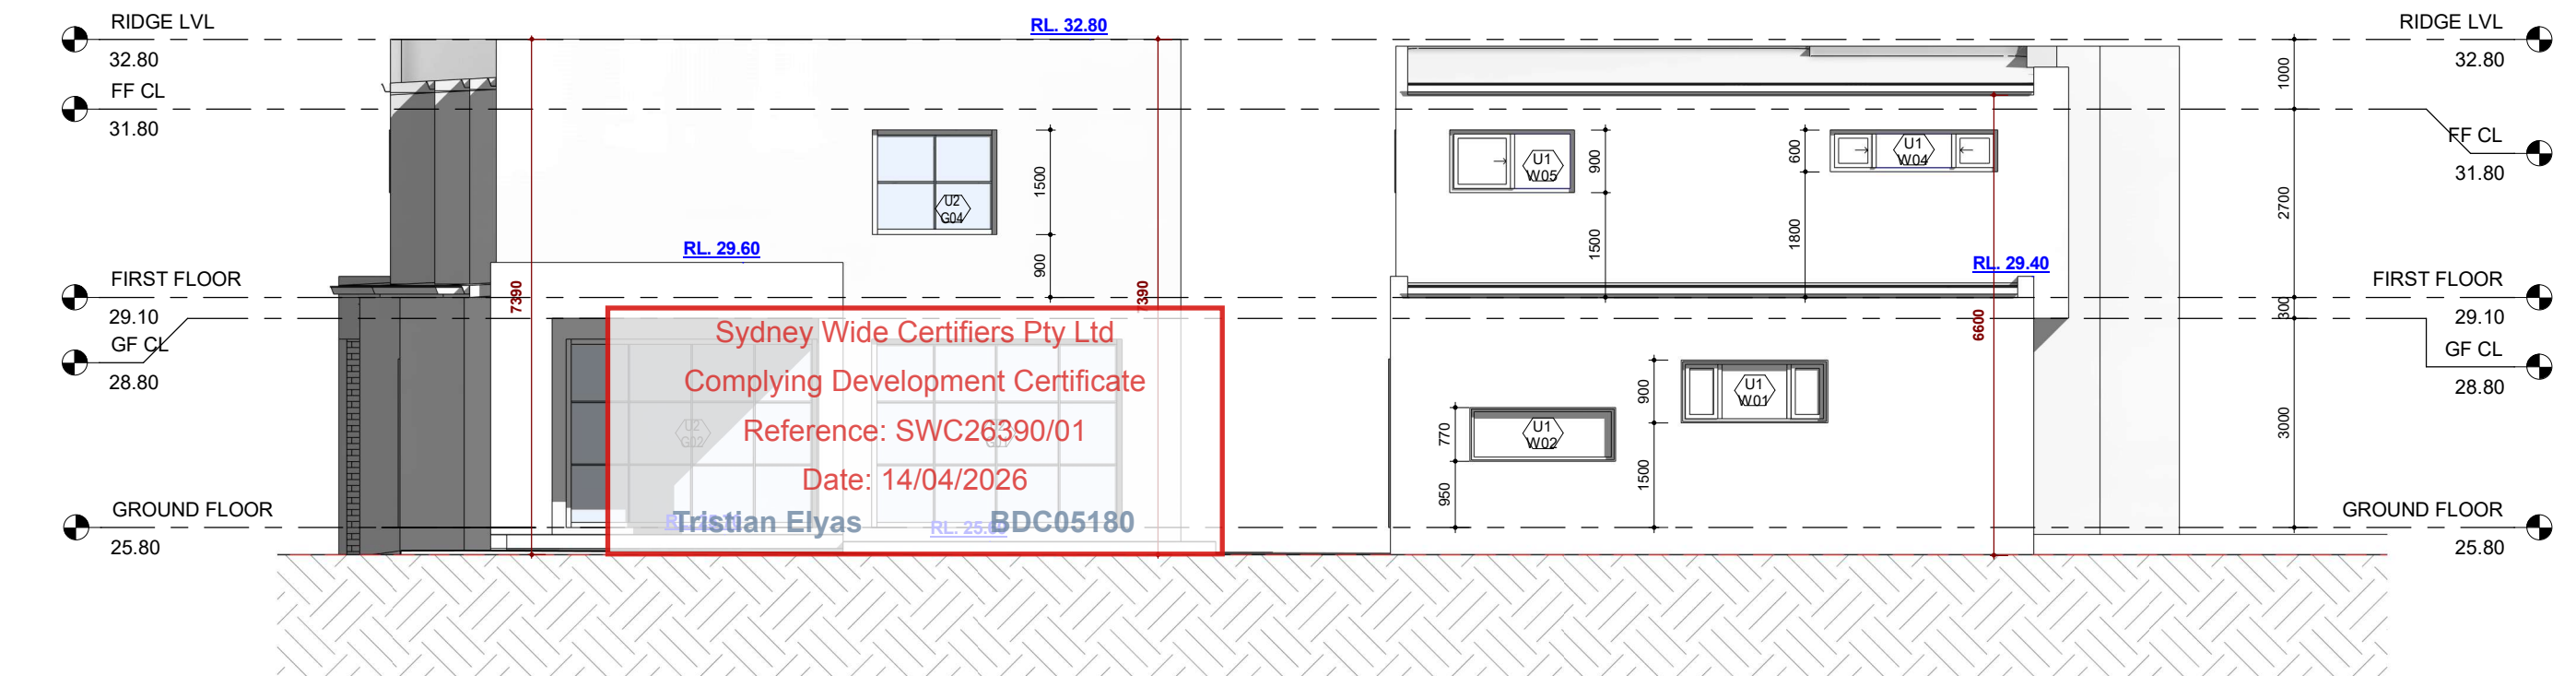

WEST ELEVATION

1 : 100

SLEIMAN

PROPERTY GROUP

bdaa

ACCREDITED

BUILDING DESIGNER

BDA Reg No. 6973

NOTE

Do not scale drawing, figured dimension only to be used.

All measurements are in millimetres.

COPYRIGHT

All rights reserved.

These drawings, plans and specifications and the copyright are the property of SLEIMAN PROPERTY GROUP and must not be used, reproduced or copied wholly or in part without the written permission of SLEIMAN PROPERTY GROUP

Northpoint

NO.	DRAWING:	BY:	DATE:	AMENDMENTS:
1	ISSUE FOR REVIEW		17/02/26	
2	ISSUE FOR CDC		13/04/26	
3				
4				
5				
6				
7				

CLIENT: DEBRA FRANCIS

ADDRESS: 42 DARTMOOR CIRCUIT EMU HEIGHTS

ELEVATIONS


Project number135

DateFEB26

Drawn byLS


A302

Scale 1 : 100

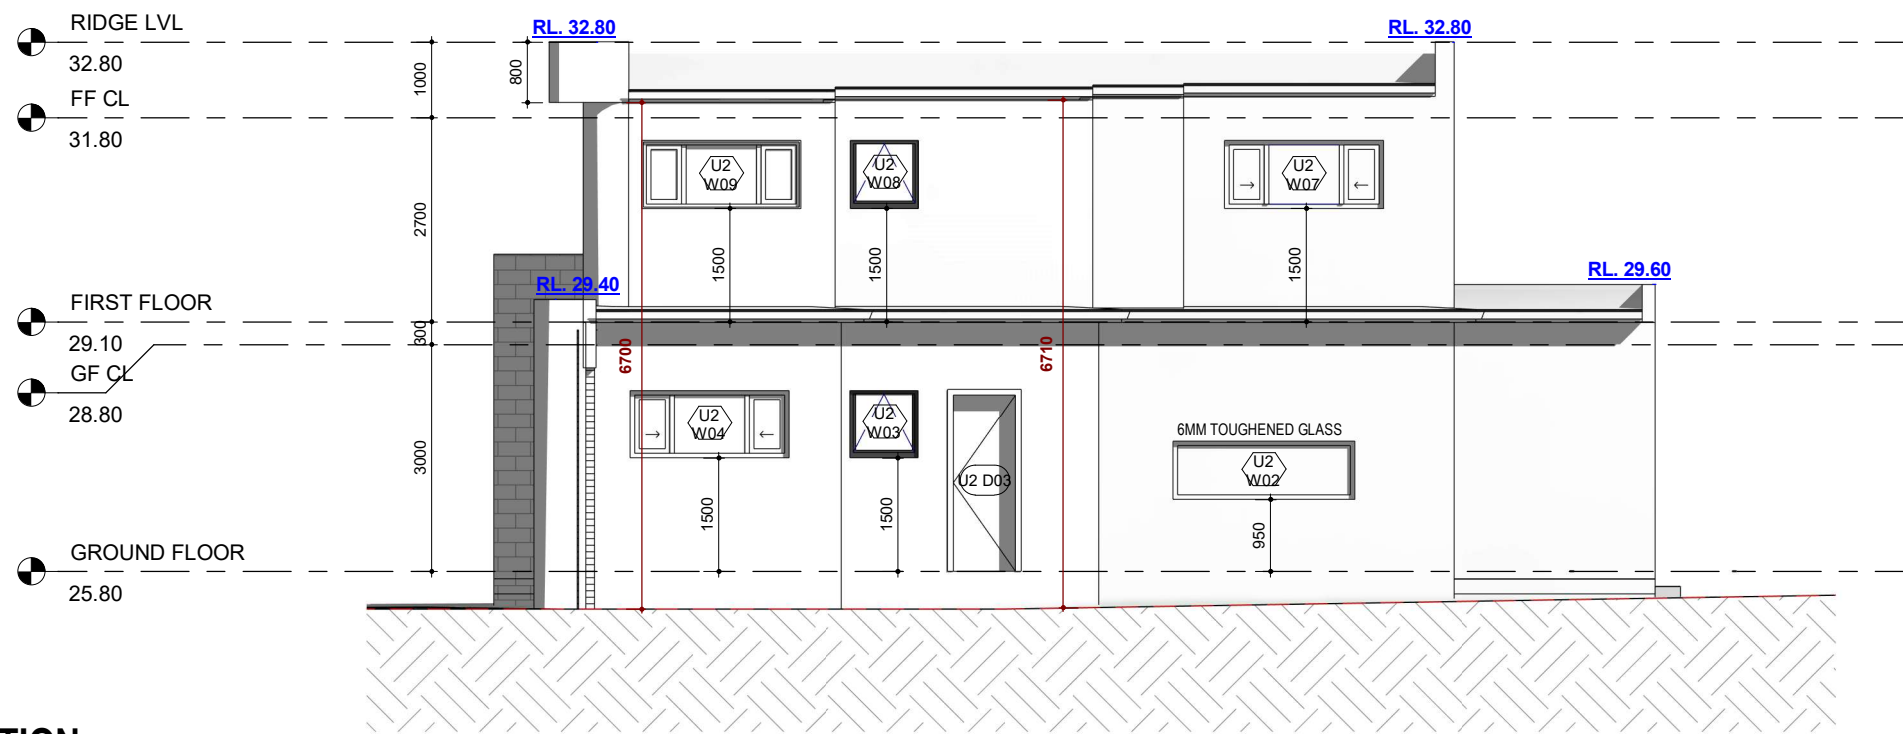

U2 NORTH ELEVATION

1 : 100

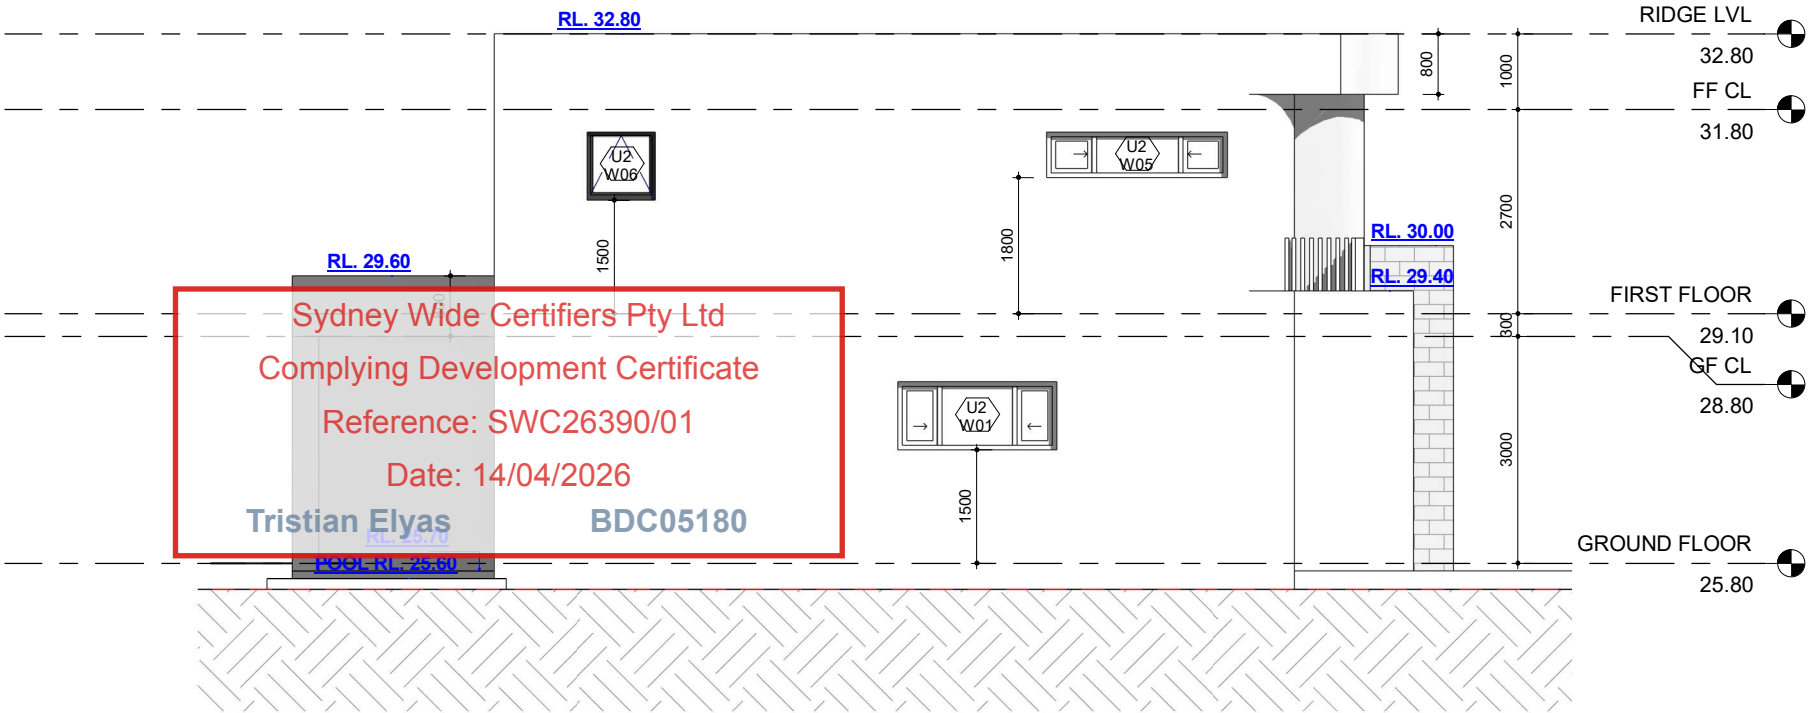

U2 SOUTH ELEVATION

1 : 100

SLEIMAN
PROPERTY GROUP

bdqa
ACCREDITED
BUILDING DESIGNER

BDAA Reg No. 6973

NOTE
Do not scale drawing, figured dimension only to be used.
All measurements are in millimetres.

COPYRIGHT
All rights reserved.
These drawings, plans and specifications and the copyright are the property
of SLEIMAN PROPERTY GROUP and must not be used, reproduced or
copied wholly or in part without the written permission of SLEIMAN
PROPERTY GROUP

Northpoint



NO.	DRAWING:	BY:	DATE:	AMENDMENTS:
1	ISSUE FOR REVIEW		17/02/26	
2	ISSUE FOR CDC		13/04/26	
3				
4				
5				
6				
7				

CLIENT: **DEBRA FRANCIS**

ADDRESS: **42 DARTMOOR CIRCUIT EMU
HEIGHTS**

ELEVATIONS

Project number 135

Date FEB26


Drawn by LS

A303

Scale 1 : 100


U1 SECTION AA

1 : 100

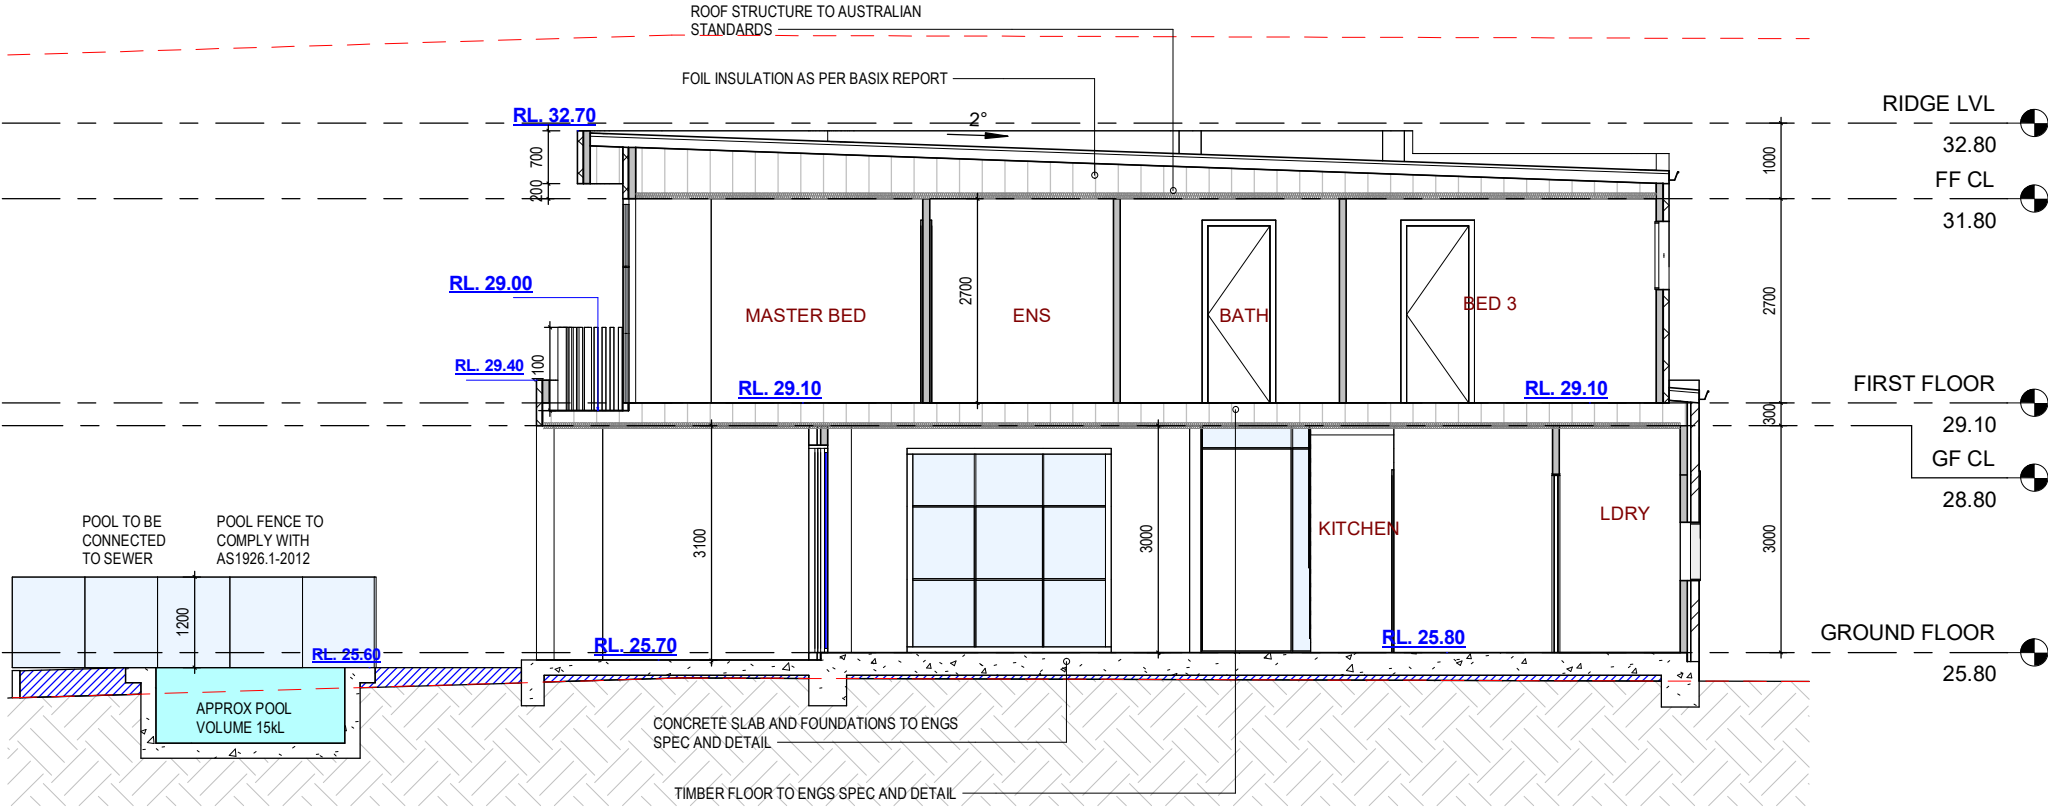

U2 SECTION AA

1 : 100

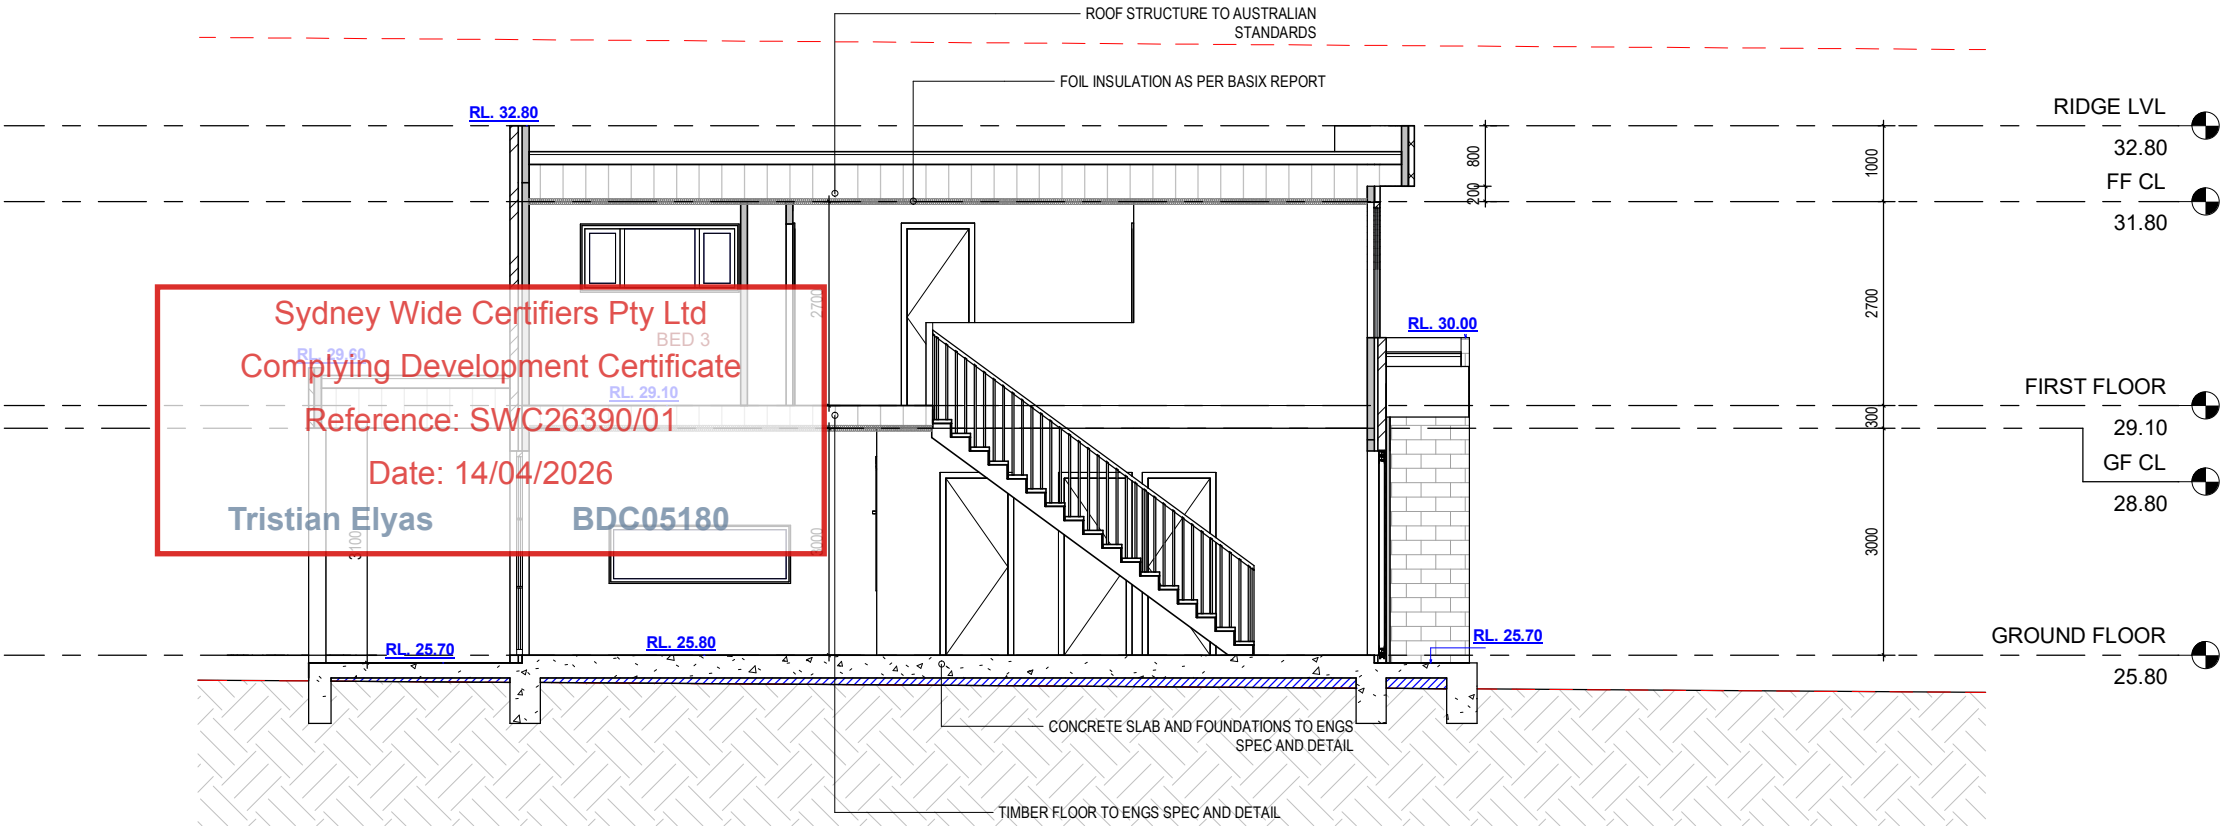

Sydney Wide Certifiers Pty Ltd
Complying Development Certificate
Reference: SWC26390/01
Date: 14/04/2026
Tristian Elyas BDC05180

SLEIMAN
PROPERTY GROUP

bdac
ACCREDITED
BUILDING DESIGNER

BDAA Reg No. 6973

NOTE
Do not scale drawing, figured dimension only to be used.
All measurements are in millimetres.

COPYRIGHT
All rights reserved.
These drawings, plans and specifications and the copyright are the property
of SLEIMAN PROPERTY GROUP and must not be used, reproduced or
copied wholly or in part without the written permission of SLEIMAN
PROPERTY GROUP

Northpoint



NO.	DRAWING:	BY:	DATE:	AMENDMENTS:
1	ISSUE FOR REVIEW		17/02/26	
2	ISSUE FOR CDC		13/04/26	
3				
4				
5				
6				
7				

CLIENT: DEBRA FRANCIS

ADDRESS: 42 DARTMOOR CIRCUIT EMU
HEIGHTS

SECTIONS


Project number 135

Date FEB26

Drawn by LS


A304

Scale 1 : 100

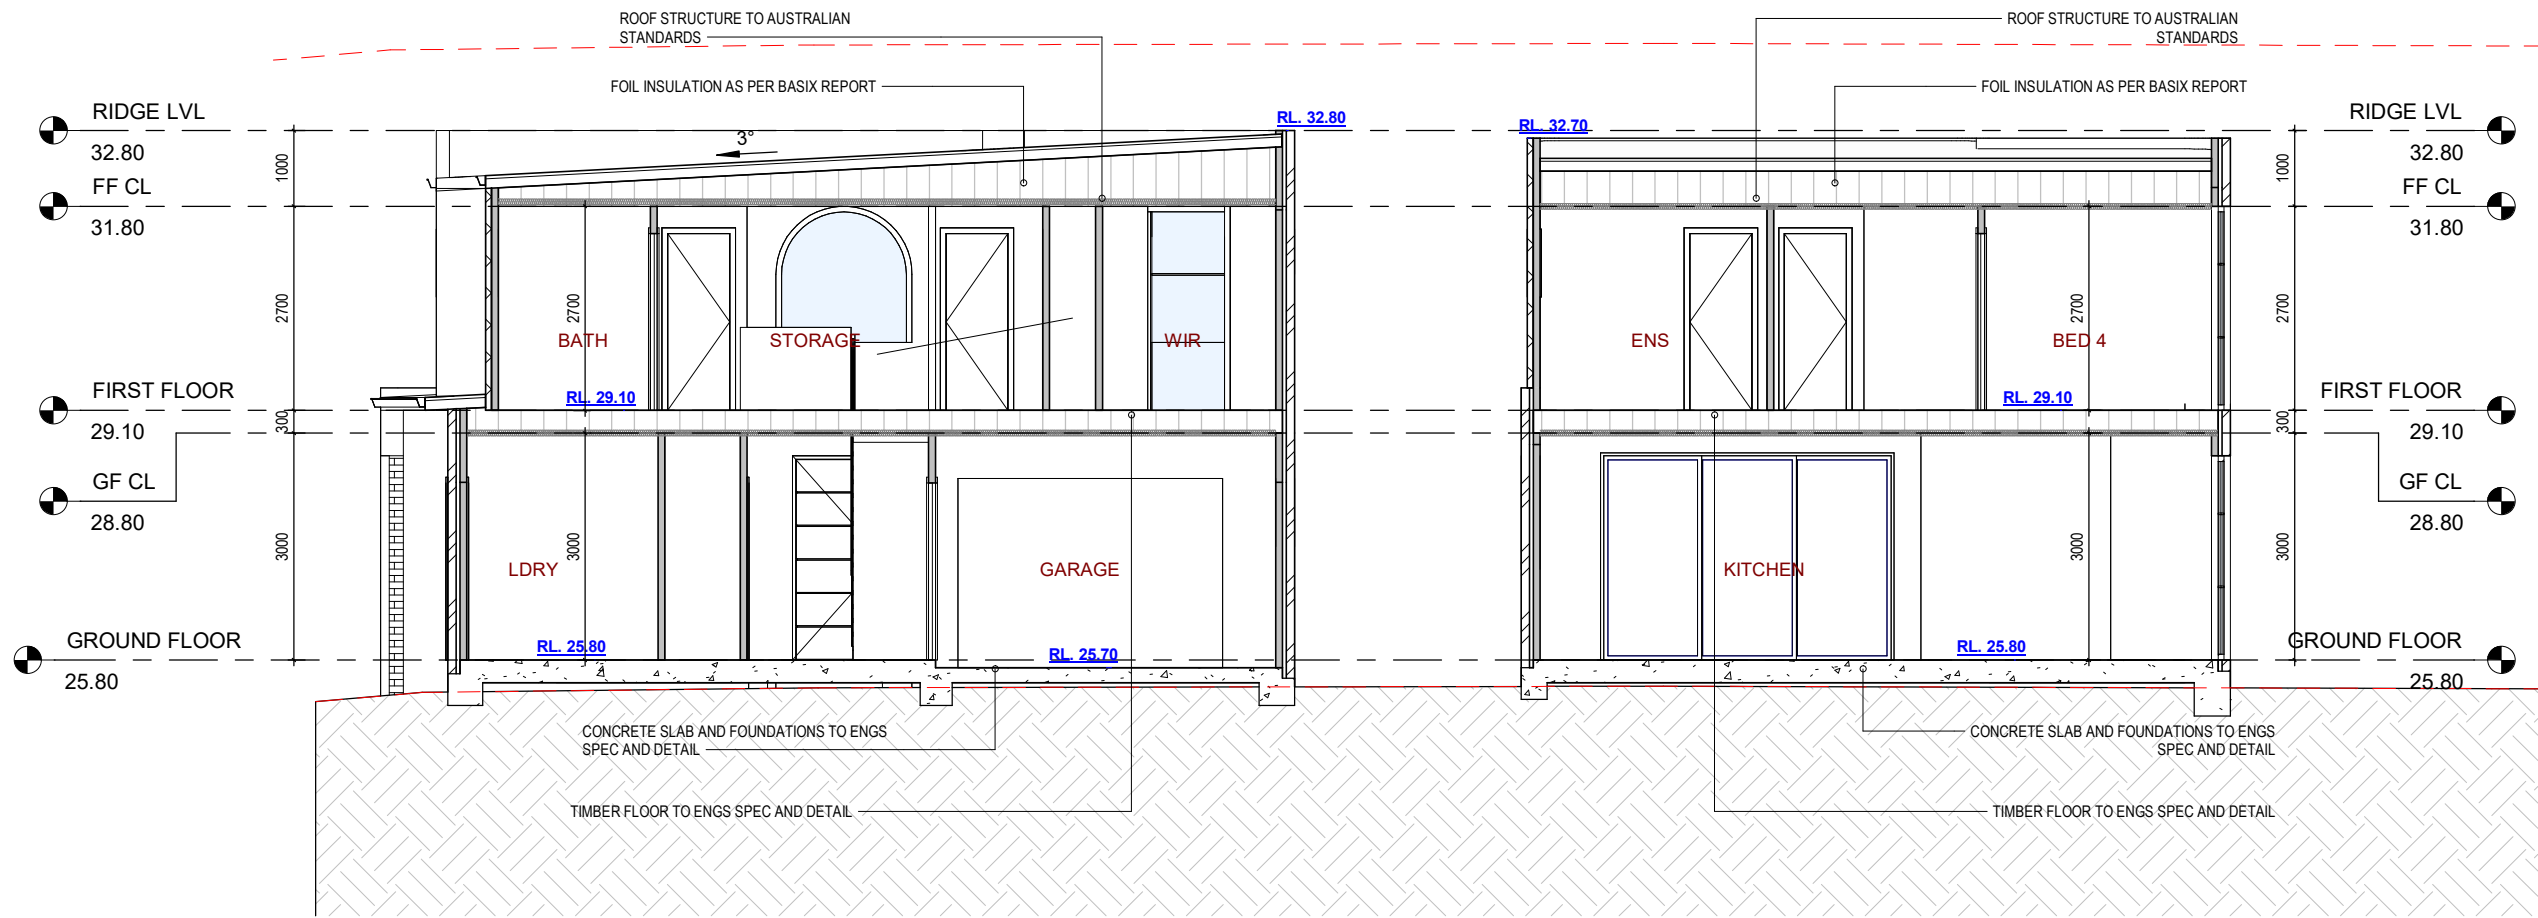

CROSS SECTION AA

1 : 100

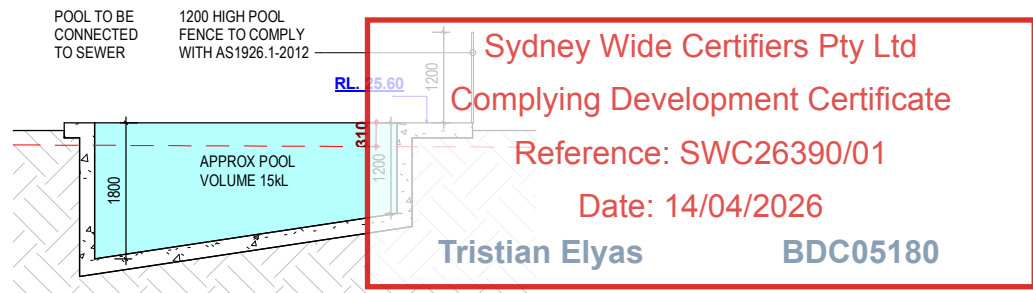

POOL SECTION

1 : 100

SLEIMAN

PROPERTY GROUP

bdaa

ACCREDITED

BUILDING DESIGNER

BDAA Reg No. 6973

NOTE

Do not scale drawing, figured dimension only to be used.

All measurements are in millimetres.

COPYRIGHT

All rights reserved.

These drawings, plans and specifications and the copyright are the property of SLEIMAN PROPERTY GROUP and must not be used, reproduced or copied wholly or in part without the written permission of SLEIMAN PROPERTY GROUP

Northpoint

NO.	DRAWING:	BY:	DATE:	AMENDMENTS:
1	ISSUE FOR REVIEW		17/02/26	
2	ISSUE FOR CDC		13/04/26	
3				
4				
5				
6				
7				

CLIENT: DEBRA FRANCIS

ADDRESS: 42 DARTMOOR CIRCUIT EMU HEIGHTS

SECTIONS

Project number	135	A305
Date	FEB26	
Drawn by	LS	

Scale 1 : 100

DOORS SCHEDULE			
MARK	HEIGHTS	WIDTH	LEVEL
U1 D01	2500	3000	GROUND FLOOR
U1 D02	2340	820	GROUND FLOOR
U1 D03	2700	3800	GROUND FLOOR
U1 D04	2340	820	GROUND FLOOR
U1 D05	2340	820	GROUND FLOOR
U1 D06	2340	800	GROUND FLOOR
U1 D07	2340	820	FIRST FLOOR
U1 D08	2340	820	FIRST FLOOR
U1 D09	2340	820	FIRST FLOOR
U1 D10	2340	820	FIRST FLOOR
U1 D11	2340	820	FIRST FLOOR
U1 D12	2340	820	FIRST FLOOR
U1 D13	2340	820	FIRST FLOOR
U2 D01	2700	1200	GROUND FLOOR
U2 D02	2500	3500	GROUND FLOOR
U2 D03	2340	820	GROUND FLOOR
U2 D04	2340	820	GROUND FLOOR
U2 D05	2340	820	GROUND FLOOR
U2 D06	2340	820	GROUND FLOOR
U2 D07	2340	820	GROUND FLOOR
U2 D08	2340	820	FIRST FLOOR
U2 D09	2340	820	FIRST FLOOR
U2 D10	2340	820	FIRST FLOOR
U2 D11	2340	820	FIRST FLOOR
U2 D12	2340	820	FIRST FLOOR
U2 D13	2340	820	FIRST FLOOR
U2 D15	2400	1040	FIRST FLOOR

Grand total: 27

WINDOWS SCHEDULE					
MARK	HEIGHT	WIDTH	SILL HEIGHT	HEAD HEIGHT	LEVEL
U1 W01	900	2100	1500	2400	GROUND FLOOR
U1 W02	770	2100	950	1720	GROUND FLOOR
U1 W03	1500	2700	1200	2700	GROUND FLOOR
U1 W04	600	2400	1800	2400	FIRST FLOOR
U1 W05	900	1800	1500	2400	FIRST FLOOR
U1 W06	900	1500	1500	2400	FIRST FLOOR
U1 W07	900	1800	1500	2400	FIRST FLOOR
U1 W08	900	2400	1500	2400	FIRST FLOOR
U2 W01	900	2100	1500	2400	GROUND FLOOR
U2 W02	770	2400	950	1720	GROUND FLOOR
U2 W03	900	900	1500	2400	GROUND FLOOR
U2 W04	900	2100	1500	2400	GROUND FLOOR
U2 W05	600	2400	1800	2400	FIRST FLOOR
U2 W06	900	900	1500	2400	FIRST FLOOR
U2 W07	900	2100	1500	2400	FIRST FLOOR
U2 W08	900	900	1500	2400	FIRST FLOOR
U2 W09	900	2100	1500	2400	FIRST FLOOR
Grand total: 17					

GLAZING SCHEDULE		
Mark	HEIGHT	WIDTH
U1 G01	2700	2700
U1 G02	6000	2400
U1 G03	2700	2700
U1 G04	2500	2100
U1 G05	2700	3845
U2 G01	2700	3600
U2 G02	2700	3600
U2 G03	2700	2500
U2 G04	1500	1800
U2 G05	2400	2500
U2 G06	1800	1800
U2 G07	2700	3135

Sydney Wide Certifiers Pty Ltd

Complying Development Certificate

Reference: SWC26390/01

Date: 14/04/2026

Tristian ElyasBDC05180

SLEIMAN

PROPERTY GROUP

bdaa

ACCREDITED

BUILDING DESIGNER

BDAA Reg No. 6973

NOTE

Do not scale drawing, figured dimension only to be used.
All measurements are in millimetres.

COPYRIGHT

All rights reserved.
These drawings, plans and specifications and the copyright are the property of SLEIMAN PROPERTY GROUP and must not be used, reproduced or copied wholly or in part without the written permission of SLEIMAN PROPERTY GROUP

Northpoint

NO.	DRAWING:	BY:	DATE:	AMENDMENTS:
1	ISSUE FOR REVIEW		17/02/26	
2	ISSUE FOR CDC		13/04/26	
3				
4				
5				
6				
7				

CLIENT: DEBRA FRANCIS	SCHEDULES	
	Project number	135
	Date	FEB26
	Drawn by	LS
ADDRESS: 42 DARTMOOR CIRCUIT EMU HEIGHTS	A401	
		Scale




COLORBOND ROOF SHEETS - DOVER WHITE OR SIMILAR



PAVING - TUSCAN TRAVERTINE OR SIMILAR



RENDERED FINISH WALLS - DULUX NATURAL WHITE OR SIMILAR

 

ALUMINIUM WINDOWS AND FRAMES - PEARL WHITE OR SIMILAR

Sydney Wide Certifiers Pty Ltd
Complying Development Certificate
Reference: SWC26390/01

Date: 14/04/2026

Tristian Elyas

BDC05180



SLEIMAN
PROPERTY GROUP

bdaa
ACCREDITED
BUILDING DESIGNER

BDAA Reg No. 6973

NOTE
Do not scale drawing, figured dimension only to be used.
All measurements are in millimetres.

COPYRIGHT
All rights reserved.
These drawings, plans and specifications and the copyright are the property
of SLEIMAN PROPERTY GROUP and must not be used, reproduced or
copied wholly or in part without the written permission of SLEIMAN
PROPERTY GROUP

Northpoint



NO.	DRAWING:	BY:	DATE:	AMENDMENTS:
1	ISSUE FOR REVIEW		17/02/26	
2	ISSUE FOR CDC		13/04/26	
3				
4				
5				
6				
7				

CLIENT: DEBRA FRANCIS

ADDRESS: 42 DARTMOOR CIRCUIT EMU
HEIGHTS

COLOUR SCHEDULE

Project number 135

Date FEB26

Drawn by LS


A402

Scale



SHADOW DIAGRAMS 9AM

1 : 500

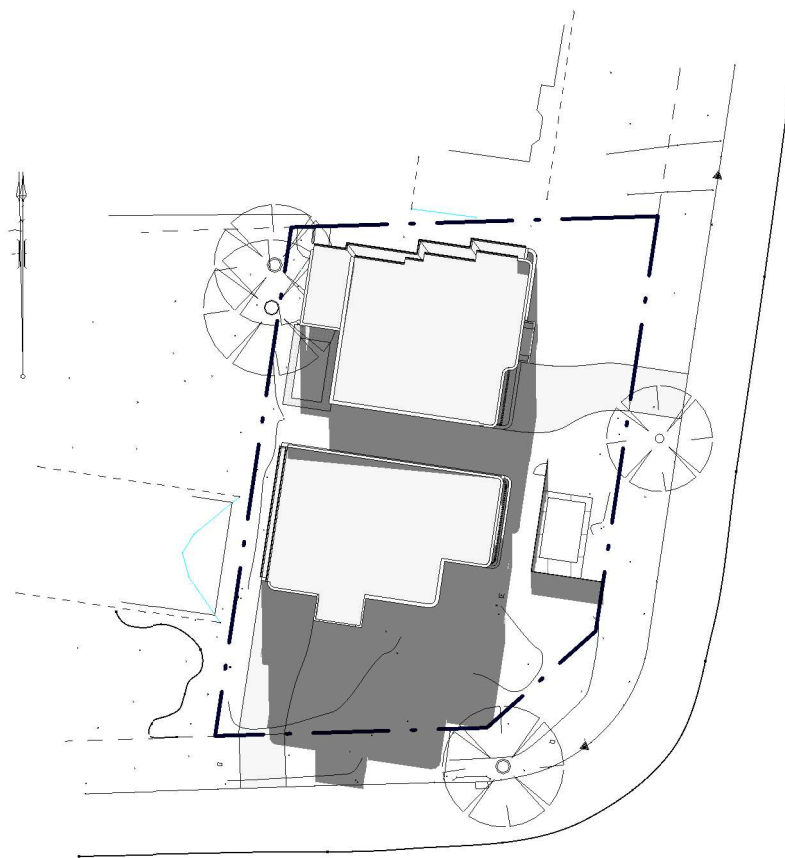

SHADOW DIAGRAMS 12PM

1 : 500



SHADOW DIAGRAMS 3PM

1 : 500

Sydney Wide Certifiers Pty Ltd
Complying Development Certificate

Reference: SWC26390/01

Date: 14/04/2026

Tristian Elyas

BDC05180

SLEIMAN
PROPERTY GROUP

bdaa
ACCREDITED
BUILDING DESIGNER

BDAA Reg No. 6973

NOTE
Do not scale drawing, figured dimension only to be used.
All measurements are in millimetres.

COPYRIGHT
All rights reserved.
These drawings, plans and specifications and the copyright are the property
of SLEIMAN PROPERTY GROUP and must not be used, reproduced or
copied wholly or in part without the written permission of SLEIMAN
PROPERTY GROUP

Northpoint



NO.	DRAWING:	BY:	DATE:	AMENDMENTS:
1	ISSUE FOR REVIEW		17/02/26	
2	ISSUE FOR CDC		13/04/26	
3				
4				
5				
6				
7				

CLIENT: DEBRA FRANCIS	SHADOW DIAGRAMS		
ADDRESS: 42 DARTMOOR CIRCUIT EMU HEIGHTS	Project number	135	A403 Scale 1 : 500
	Date	FEB26	
	Drawn by	Author	

LANDSCAPE PLAN

1 : 200

SLEIMAN

PROPERTY GROUP

bdaa

ACCREDITED

BUILDING DESIGNER

BDA Reg No. 6973

NOTE

Do not scale drawing, figured dimension only to be used.

All measurements are in millimetres.

COPYRIGHT




All rights reserved.

These drawings, plans and specifications and the copyright are the property of SLEIMAN PROPERTY GROUP and must not be used, reproduced or copied wholly or in part without the written permission of SLEIMAN PROPERTY GROUP


Northpoint

NO.	DRAWING:	BY:	DATE:	AMENDMENTS:
1	ISSUE FOR REVIEW		17/02/26	
2	ISSUE FOR CDC		13/04/26	
3				
4				
5				
6				
7				

CLIENT: DEBRA FRANCIS	LANDSCAPE PLAN	
ADDRESS: 42 DARTMOOR CIRCUIT EMU HEIGHTS	Project number	135
	Date	FEB26
	Drawn by	Author
		A501
		SAs indicated

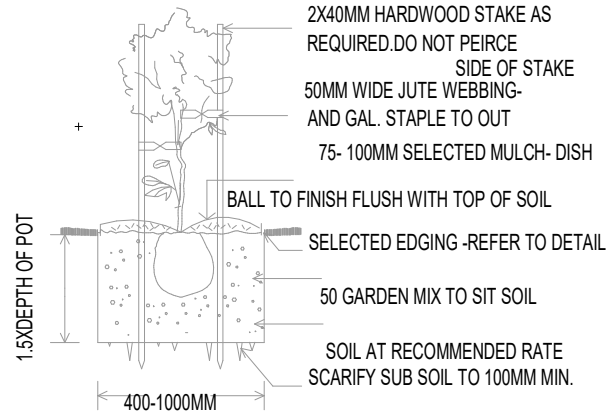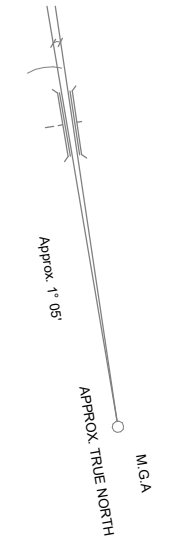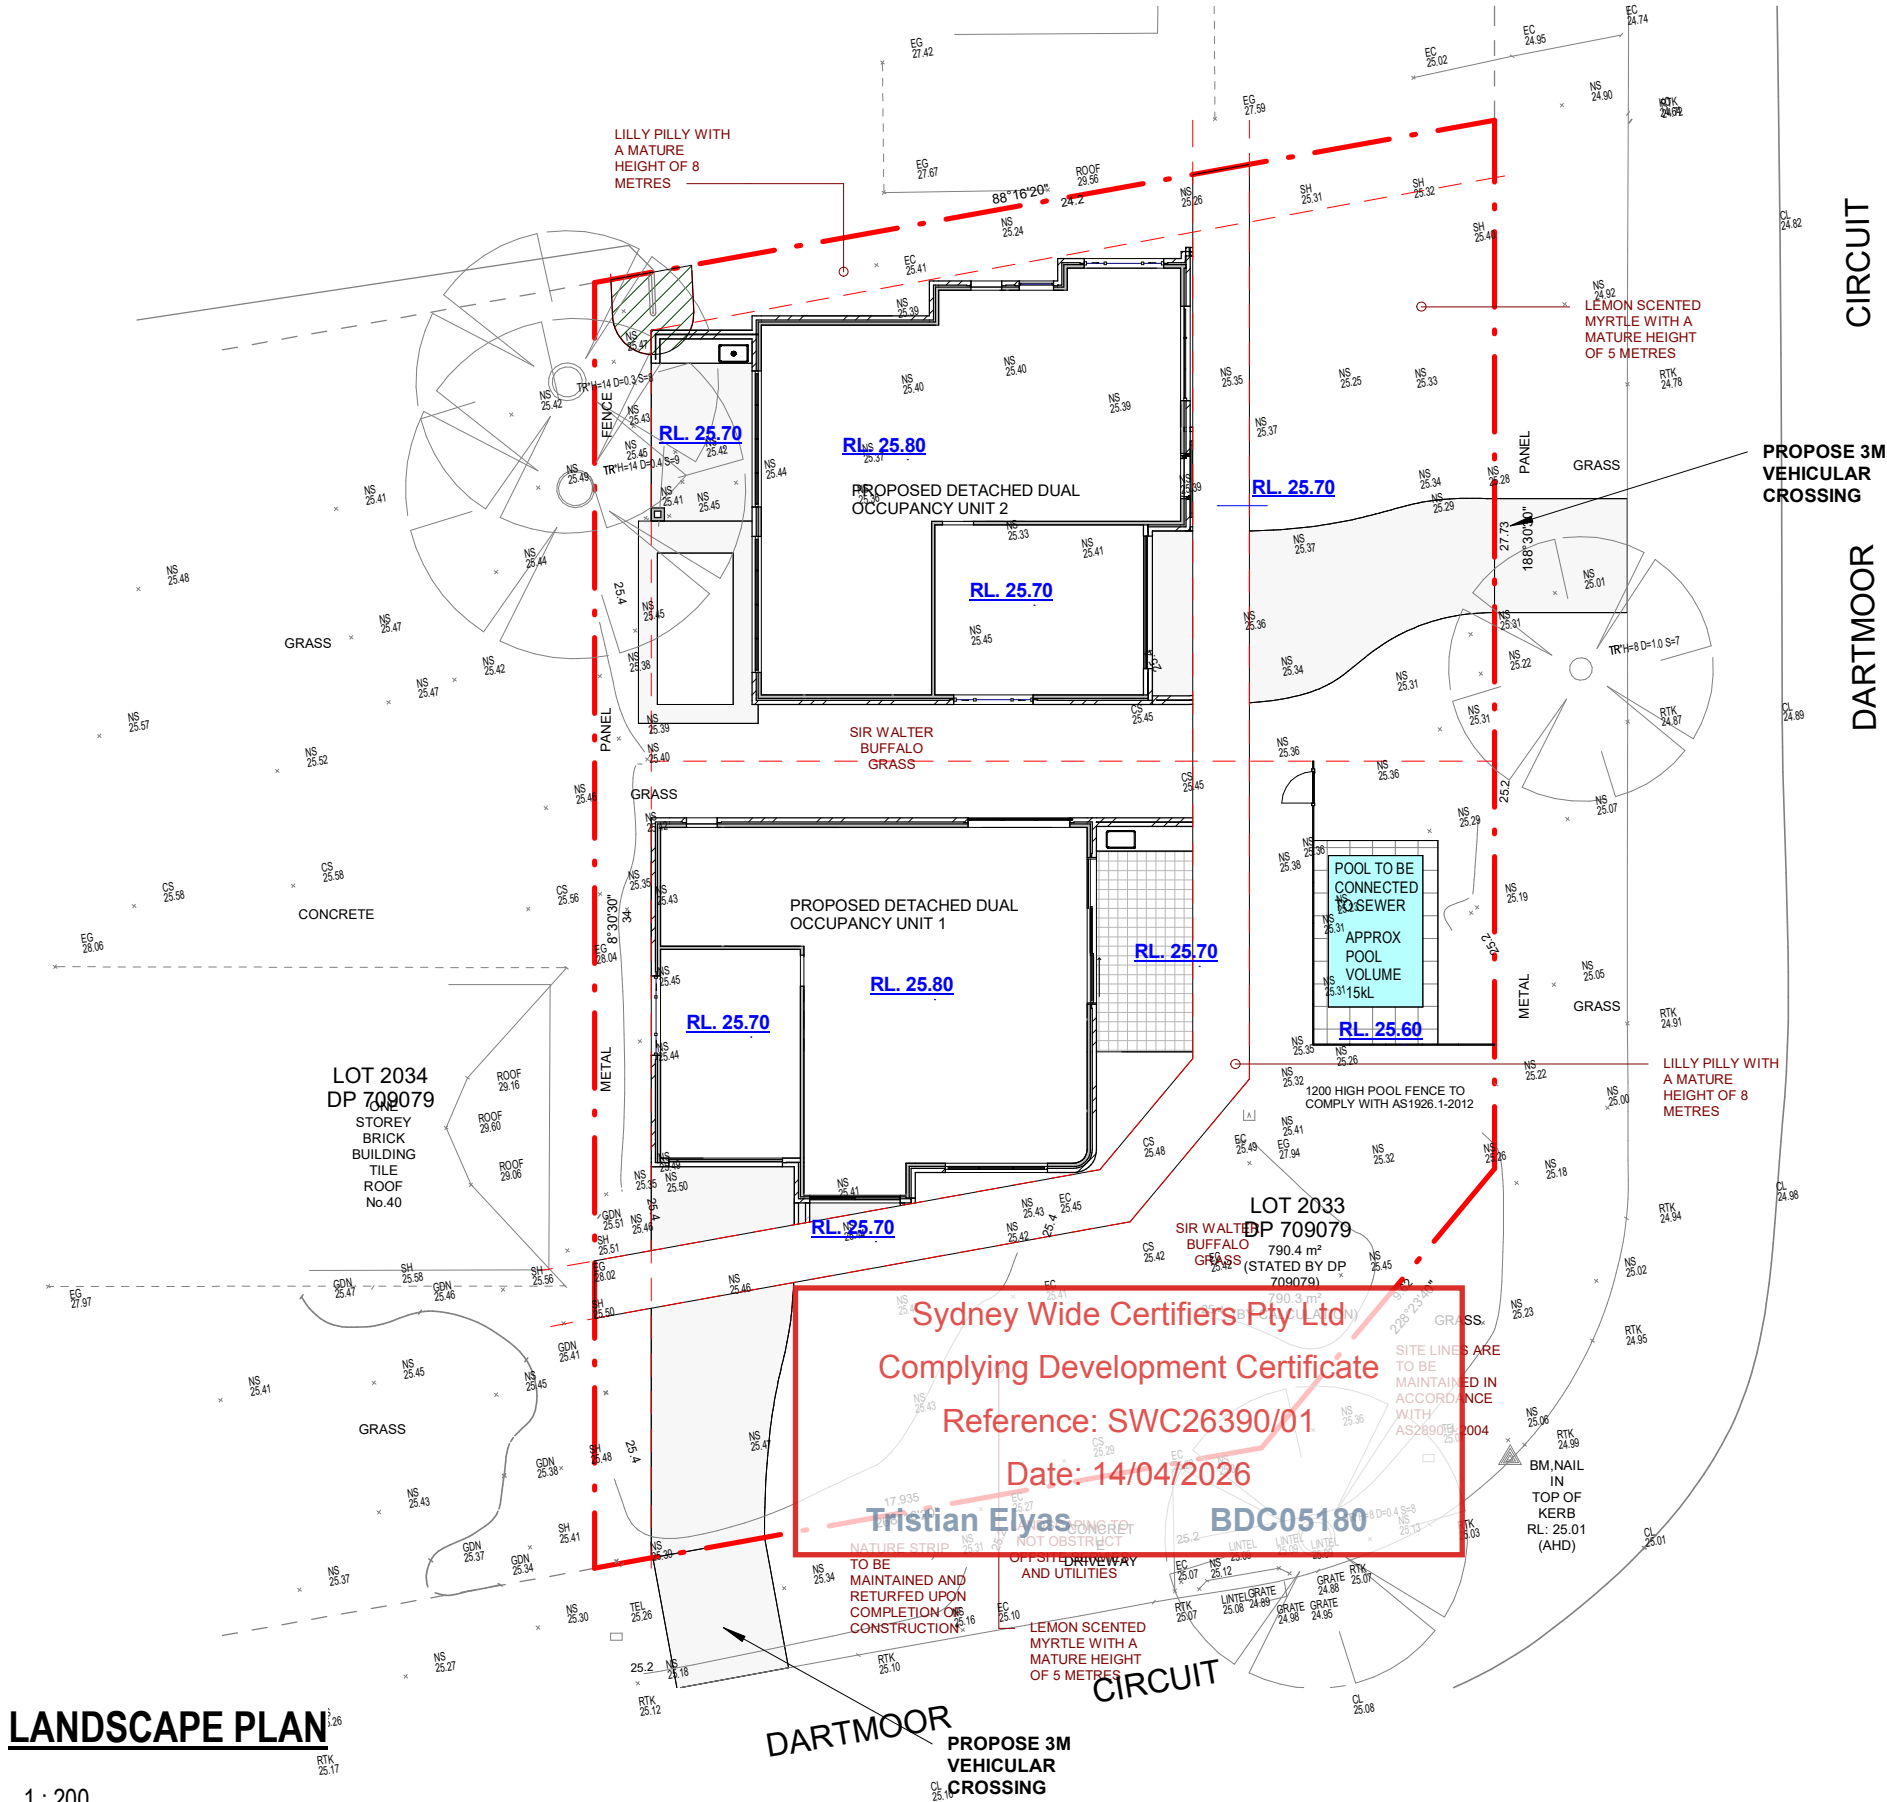

25 - 75 litre Typical Tree planting
Detail: Not To Scale

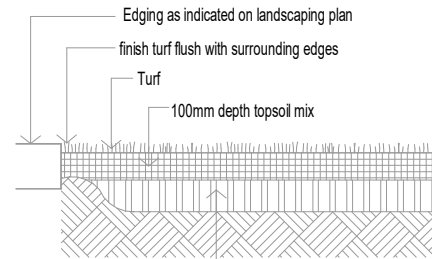

Ground preparation (Grass area- turf)
Detail: Not To Scale

PLANTING AND MAINTENANCE NOTES:

PLANTING MIX:
Imported planting mix to planting beds is to comprise of an approved soil mix of: 1. 60% soil mix (75% coars and 25% back soil), 2. 10% mushroom compost, 3. 10% composted sawdust, 4. 10% pine bark, 5. 10% compost manure

Mulch:
- Much shall be hardwood chip mulch tree from exotic plant material

Plant Material:
- All plants shall be free of fungus and insect damage, all plants shall be healthy, well shaped, not soft or force frown and not root bound,

Turfed Areas:
- All new turfed areas are to be selected weed free Sir Walter Buffalo.
- Turf shall be laid neatly with staggered joins, flush with adjacent surfaces and have even running falls to all drainage points.

Maintenance/Plant Establishment:
- Landscaping contractors to provide 13 weeks for maintenance/plant establishment period, carry out recurrent works of maintenance nature including, but not limited to: watering, mowing, weeding, rubbish removal, fertilising, pest and disease control, returfing, staking, and tying, replanting, cultivating, pruning, hedge clipping, top dressing, and keep the site neat and tidy.

Common Name	Native Name	Mature Height	Mature Spread
Lilly Pilly (Creek Lilly Pilly)	Acmena smithii (Syzygium smithii)	8-10 m	3-6 m
Lemon Scented Myrtle	Backhousia citriodora	3-5 m	2-3 m

LANDSCAPE DETAILS

1 : 100