

FOR CONSTRUCTION

LOT 15 29 DEW STREET AUSTRAL
PROPOSED CONSTRUCTION OF A TWO STOREY DWELLING



BASIX COMMITMENTS		Certificate number: 1864160S_02 Date of issue: Monday, 07 September 2026
WATER		
LANDSCAPE	74m2	
TOILETS	4 STARS	
KITCHEN TAPS	4 STARS	
SHOWER HEADS	4 STAR (>4.5 but <=6 Umin)	
BASIN TAPS	4 STARS	
ALTERNATIVE WATER	1500L RAINWATER TANK	
ROOF WATER TO TANK	176m2	
ALT.WATER USES- TANK	LAUNDRY	
ALT. WATER USES - RETIC	ALL TOILETS + ONE OUTDOOR TAP	
OUTDOOR SPA	NA	
ENERGY		
HOT WATER	GAS INSTANTANEOUS - 7 STAR	
AIR-CON (HEATING)	3 PHASE DUCTED - EER 3.0-3.5	
AIR-CON (COOLING)	3 PHASE DUCTED - EER 3.0-3.5	
VENTILATION - BATHROOM	INTERLOCKED WITH LIGHT	
VENTILATION - KITCHEN	DUCTED - MANUAL SWITCH	
VENTILATION - LAUNDRY	NONE/ NATURAL VENTILATION	
PV SYSTEM	NA	
COOKTOP	GAS	
OVEN	ELECTRIC	
CLOTHES DRYING	OUTDOOR CLOTHESLINE	
LIGHTING	DEDICATED LED	

GENERAL LEGEND

AC	AIR CONDITIONING UNIT
AL	POWDERCOATED ALUMINIUM DOOR/ WINDOW
BAL	BALUSTRADE TYPE
BG	BOX GUTTER
BR1, BR2, etc.	BRICK FACE TYPE
CAP	METAL CAPPING
CD1, CD2, etc.	WALL CLADDING
CONC.	CONCRETE FLOOR
CPT	CARPET
CRT	CONCRETE ROOF TILES
CR1, CR2, etc.	CEMENT RENDER TYPE/ COLOUR
DP/S	DOWN PIPE
DW	DISH WASHER
ED	ENTRY DOOR
F	FRIDGE
FAS	FASCIA
FET	FEATURE TILE
FT, FT1, FT2, etc.	FLOOR TILES
FW	FLOOR WASTE
GD	GARAGE DOOR
GUT	GUTTER
HWU	HOT WATER UNIT
HYB	HYBRID FLOOR
L	LINEN
MR	METAL ROOF
MW	MICROWAVE OVEN
NGL	NATURAL GROUND LEVEL
OBS	OBSCURED GLASS
P	PANTRY
R	ROBE
RL	REDUCED LEVEL
RWH	RAIN WATER HEAD
RWT	RAIN WATER TANK
S	STORAGE
TOW	TOP OF WALL
TL	TIMBER LAMINATE
WC	WATER CLOSET
WM	WASHING MACHINE
SD	SMOKE DETECTOR

Sheet List				
Sheet No.	Sheet Name	Drawn By	Current Revision Date	Current Revision
CDC.01	COVER SHEET	AS	20-08-2025	CDC ISSUE
CDC.02A	GENERAL NOTES	AS	20-08-2025	CDC ISSUE
CDC.2B	GENERAL NOTES	AS	20-08-2025	CDC ISSUE
CDC.03	LOCATION PLAN AND SITE PLAN	AS	20-08-2025	CDC ISSUE
CDC.04	SITE ANALYSIS AND SEDIMENT CONTROL	AS	20-08-2025	CDC ISSUE
CDC.05	GROUND FLOOR PLAN	AS	20-08-2025	CDC ISSUE
CDC.06	FIRST FLOOR LEVEL	AS	20-08-2025	CDC ISSUE
CDC.07	ROOF PLAN	AS	20-08-2025	CDC ISSUE

Sheet List				
Sheet No.	Sheet Name	Drawn By	Current Revision Date	Current Revision
CDC.08	ELEVATION 01	AS	20-08-2025	CDC ISSUE
CDC.09	ELEVATION 02	AS	20-08-2025	CDC ISSUE
CDC.10	SECTIONS	AS	20-08-2025	CDC ISSUE
CDC.11	FLOOR AREA PLAN	AS	20-08-2025	CDC ISSUE
CDC.12	RENTABLE AREA PLAN	AS	20-08-2025	CDC ISSUE
CDC.14	COLOR SCHEDULE	AS	20-08-2025	CDC ISSUE
CDC.15	LANDSCAPE PLAN	AS	20-08-2025	CDC ISSUE
CDC.16	WATERPROOFING DETAILS	AS	20-08-2025	CDC ISSUE

NOTE.: ALL IMAGES ARE FOR ILLUSTRATION ONLY AND ARE SUBJECT TO VARIATION AND TO AVAILABILITY OF MATERIALS.

6	20-08-2025	CDC ISSUE	
5	04-07-2025	Revision 5	
4	27-06-2025	Revision 4	
3	24-06-2025	Revision 3	
2	24-07-2025	Revision 2	
1	16-07-2025	Concept Issue	
REV	DATE	DESCRIPTION	BY



THIS DRAWING IS THE EXCLUSIVE PROPERTY OF THE DEVELOPER & THE REPRODUCTION OF ANY PART WITHOUT THE PRIOR WRITTEN CONSENT OF THE DEVELOPER IS A VIOLATION OF APPLICABLE LAWS. IN NO EVENT SHALL THE DEVELOPER BE HELD LIABLE FOR SPECIAL COLLATERAL, INCIDENTAL OR CONSEQUENTIAL LIABILITY IN CONNECTION WITH THE USE OF THIS DIGITAL DATA ONCE RELEASED FROM THE DEVELOPER'S OFFICE. THIS DRAWING IS TO BE READ & UNDERSTOOD IN CONJUNCTION WITH THE STRUCTURAL, MECHANICAL, ELECTRICAL & / OR ANY OTHER CONSULTANT'S DOCUMENTATION AS MAY BE APPLICABLE TO THE PROJECT PRIOR TO THE START OF ANY WORKS AND FOR ITS DURATION.

PROJECT:
29 DEW STREET
AUSTRAL
LOT 15 29 DEW STREET
AUSTRAL

DRAWING TITLE:
COVER SHEET

NORTH:

LOT NO:
15
DRAWN BY:
AS
DRAFTED BY:
SL

DATE:
7-09-2026
CHECKED BY:
RH

SCALE:
As indicated

DRAWING No:
CDC.01

REV:
6
ISSUED BY:

CLIENT NAME:
Abigail & Bhinkosi Thembinkosi Madondo

A3

BUILDING SPECIFICATIONS

**National Construction Code – Volume 2,
Amendment 1 – Building Code of Australia 2022
& Housing Provisions Standard 2022**

SITE PREPARATION

- PART 3.1 OF THE NCC VOLUME 2, AMENDMENT 1 - BUILDING CODE OF AUSTRALIA 2022 & HOUSING PROVISIONS STANDARD 2022

EARTHWORKS

- TO BE CARRIED OUT IN ACCORDANCE WITH THE REQUIREMENTS OF THE ENVIRONMENTAL PLANNING & ASSESSMENT ACT 1979 AND DEVELOPMENT CONSENT CONDITIONS
- PART 3.2 OF THE NCC VOLUME 2, AMENDMENT 1 - BUILDING CODE OF AUSTRALIA 2022 & HOUSING PROVISIONS STANDARD 2022.
- AS 4678:2002 - EARTH-RETAINING STRUCTURES

DRAINAGE

- PART 3.3 OF THE NCC VOLUME 2, AMENDMENT 1 - BUILDING CODE OF AUSTRALIA 2022 & HOUSING PROVISIONS STANDARD 2022.
- AS/NZS 3500.1:2021 - PLUMBING & DRAINAGE - WATER SERVICES
- AS/NZS 3500.2:2021 - PLUMBING & DRAINAGE - SANITARY PLUMBING & DRAINAGE
- AS/NZS 3500.3:2021 - PLUMBING & DRAINAGE - STORMWATER DRAINAGE
- AS/NZS 3500.4:2021 - PLUMBING & DRAINAGE - HEATED WATER SERVICES

STRUCTURAL WORK

- Part 2.2 OF THE NCC VOLUME 2, AMENDMENT 1 - BUILDING CODE OF AUSTRALIA 2022 & HOUSING PROVISIONS STANDARD 2022.
- AS 4100:2020 - STEEL STRUCTURES CODES
- AS/NZS 1170.0:2002 - GENERAL PRINCIPLES
- AS/NZS 1170.1:2002 - PARTS 1 PERMANENT, IMPOSED AND OTHER ACTIONS
- AS/NZS 1170.2:2021 - PART 2 WIND ACTIONS
- AS 3700:2018 - SAA MASONRY CODE
- AS 1684.3:2021 - RESIDENTIAL TIMBER FRAMED CONSTRUCTION

FOOTINGS & SLABS

- PART 4 OF THE NCC VOLUME 2, AMENDMENT 1 - BUILDING CODE OF AUSTRALIA 2022 & HOUSING PROVISIONS STANDARD 2022.
- AS 2159:2009 - PILING - DESIGN & INSTALLATION
- AS 2870:2011 - RESIDENTIAL SLABS & FOOTINGS
- AS 3600:2018 - CONCRETE STRUCTURES

MASONRY

- PART 5 OF THE NCC VOLUME 2, AMENDMENT 1 - BUILDING CODE OF AUSTRALIA 2022 & HOUSING PROVISIONS STANDARD 2022.
- AS 3700:2018 - MASONRY STRUCTURES
- PART 6 OF THE NCC VOLUME 2, AMENDMENT 1 - BUILDING CODE OF AUSTRALIA 2022 & HOUSING PROVISIONS STANDARD 2022.
- AS 1684.2:2021 - RESIDENTIAL TIMBER-FRAMED CONSTRUCTION - NON- CYCLONIC AREAS
- AS 1720.1:2010 - TIMBER STRUCTURES - DESIGN METHODS
- AS 4100:2020 - STEEL STRUCTURES
- AS 3660.1:2014 - TERMITE MANAGEMENT SYSTEM

ROOF & WALL CLADDING

- PART 7 OF THE NCC VOLUME 2, AMENDMENT 1 - BUILDING CODE OF AUSTRALIA 2022 & HOUSING PROVISIONS STANDARD 2022.
- AS 1273:1991 - UNPLASTICIZED PVC (UPVC) DOWNPIPES & FITTINGS FOR RAINWATER
- AS 1562.1:2018 - DESIGN & INSTALLATION OF SHEET ROOF & WALL CLADDING - METAL
- AS/NZS 1562.3:2006 - DESIGN & INSTALLATION OF SHEET ROOF & WALL CLADDING - PLASTIC
- AS 2049:2002 - ROOF TILES
- AS 2050:2018 - INSTALLATION OF ROOF TILES
- AS 4285:2019 - ROOFLIGHTS

GLAZING

- PART 8 OF THE NCC VOLUME 2, AMENDMENT 1 - BUILDING CODE OF AUSTRALIA 2022 & HOUSING PROVISIONS STANDARD 2022.
- AS 1288:2021 - GLASS IN BUILDINGS - SELECTION & INSTALLATION
- AS 2047:2014 - WINDOWS & EXTERNAL GLAZED DOORS IN BUILDINGS
- AS/NZS 2208:1996 - SAFETY GLAZING MATERIALS IN BUILDINGS

FIRE SAFETY

- PART 9 OF THE NCC VOLUME 2, AMENDMENT 1 - BUILDING CODE OF AUSTRALIA 2022 & HOUSING PROVISIONS STANDARD 2022.
- AS 3786:2014 - SMOKE ALARMS USING SCATTERED LIGHT, TRANSMITTED LIGHT OR IONIZATION

HEALTH & AMENITY

- PART 10 OF THE NCC VOLUME 2, AMENDMENT 1 - BUILDING CODE OF AUSTRALIA 2022 & HOUSING PROVISIONS STANDARD 2022.
- AS/NZS ISO 717.1:2004 - ACOUSTICS - RATING OF SOUND INSULATION IN BUILDINGS & OF BUILDING ELEMENTS - AIRBORNE SOUND INSULATION
- AS ISO 717.2:2004 - ACOUSTICS - RATING OF SOUND INSULATION IN BUILDINGS & OF BUILDING ELEMENTS - IMPACT SOUND INSULATION
- AS 1668.2:2012 - THE USE OF VENTILATION & AIR CONDITIONING IN BUILDINGS - MECHANICAL VENTILATION IN BUILDINGS
- AS 1668.4:2012 - THE USE OF VENTILATION & AIR CONDITIONING IN BUILDINGS - NATURAL VENTILATION OF BUILDINGS
- AS/NZS 1680.0:2009 - INTERIOR LIGHTING - SAFE MOVEMENT
- AS 3740:2021 - WATERPROOFING OF DOMESTIC WET AREAS
- AS 3000:2018 - ELECTRICAL INSTALLATION
- BCA Part 10.8.1, AS4200.1 & AS4200.2 - PLIABLE BUILDING MEMBRANE INSTALLED.

WATERPROOFING

- PART 10.2 OF THE NCC VOLUME 2, AMENDMENT 1 - BUILDING CODE OF AUSTRALIA 2022 & HOUSING PROVISIONS STANDARD 2022
- AS 3740:2021 - WATERPROOFING TO WET AREA
- AS 4654:2012 - EXTERNAL WET AREAS

SAFE MOVEMENT & ACCESS

- PART 11 OF THE NCC VOLUME 2, AMENDMENT 1 - BUILDING CODE OF AUSTRALIA 2022 & HOUSING PROVISIONS STANDARD 2022.
- AS 1428.1:2009 - DESIGN FOR ACCESS & MOBILITY - GENERAL REQUIREMENTS FOR ACCESS - NEW BUILDING WORK
- AS 1657:2018 - FIXED PLATFORMS, WALKWAYS, STAIRWAYS & LADDERS - DESIGN, CONSTRUCTION & INSTALLATION

HANDRAILS & BALUSTRADE

- PART 11.3.3 OF THE NCC VOLUME 2, AMENDMENT 1 - BUILDING CODE OF AUSTRALIA 2022 & HOUSING PROVISIONS STANDARD 2022.
- PART 11.3.4 OF THE NCC VOLUME 2, AMENDMENT 1 - BUILDING CODE OF AUSTRALIA 2022 & HOUSING PROVISIONS STANDARD 2022.
- PART 11.3.5 OF THE NCC VOLUME 2, AMENDMENT 1 - BUILDING CODE OF AUSTRALIA 2022 & HOUSING PROVISIONS STANDARD 2022.
- AS 1170.1:2002 - BALUSTRADE INSTALLATION

PROTECTION OF OPENABLE WINDOW


PART 11.3.7 AND 11.3.8 OF THE NCC VOLUME 2, AMENDMENT 1 - BUILDING CODE OF AUSTRALIA 2022 & HOUSING PROVISIONS STANDARD 2022.

ENERGY EFFICIENCY

- PART 13 OF THE NCC VOLUME 2, AMENDMENT 1 - BUILDING CODE OF AUSTRALIA 2022 & HOUSING PROVISIONS STANDARD 2022 & BASIX CERTIFICATE.

MECHANICAL VENTILATION

- EXHAUST FROM A BATHROOM, SANITARY COMPARTMENT TO DISCHARGE DIRECTLY TO OUTDOOR AIR WITH MINIMUM FLOW RATE OF 25L/S & MAKE-UP AIR VIA OPENINGS TO AN ADJACENT ROOM WITH A FREE AREA OF 14,000 MM². THIS EXHAUST SYSTEM MUST BE INTERLOCKED WITH LIGHT SWITCH AND INCLUDE RUN-ON TIMER SO THAT THE EXHAUST SYSTEM CONTINUES TO OPERATE FOR 10 MINUTES AFTER THE LIGHT SWITCH IS OFF.
- ANY INSTALLED - KITCHEN RANGEHOOD EXHAUST TO DISCHARGE DIRECTLY OR VIA DUCT TO OUTDOOR AIR WITH MINIMUM FLOW RATE OF 40L/S & MAKE-UP AIR VIA OPENINGS TO AN ADJACENT ROOM WITH A FREE AREA OF 14,000 MM².
- LAUNDRY EXHAUST TO DISCHARGE DIRECTLY OR VIA DUCT TO OUTDOOR AIR WITH MINIMUM FLOW RATE OF 40L/S & MAKE-UP AIR VIA OPENINGS TO AN ADJACENT ROOM WITH A FREE AREA OF 14,000 MM².

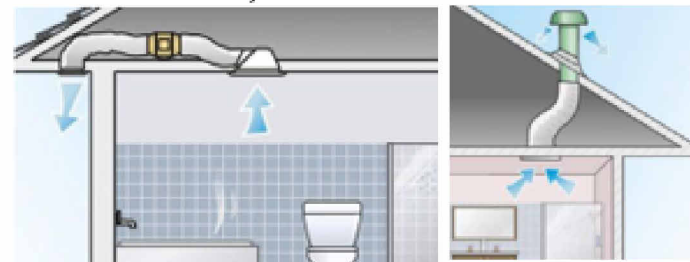

REV	DATE	DESCRIPTION	BY
6	20-08-2025	CDC ISSUE	



THIS DRAWING IS THE EXCLUSIVE PROPERTY OF THE DEVELOPER & THE REPRODUCTION OF ANY PART WITHOUT THE PRIOR WRITTEN CONSENT OF THE DEVELOPER IS A VIOLATION OF APPLICABLE LAWS. IN NO EVENT SHALL THE DEVELOPER BE HELD LIABLE FOR SPECIAL COLLATERAL, INCIDENTAL OR CONSEQUENTIAL LIABILITY IN CONNECTION WITH THE USE OF THIS DIGITAL DATA ONCE RELEASED FROM THE DEVELOPER'S OFFICE. THIS DRAWING IS TO BE READ & UNDERSTOOD IN CONJUNCTION WITH THE STRUCTURAL, MECHANICAL, ELECTRICAL & / OR ANY OTHER CONSULTANT'S DOCUMENTATION AS MAY BE APPLICABLE TO THE PROJECT PRIOR TO THE START OF ANY WORKS AND FOR ITS DURATION.

PROJECT:
29 DEW STREET
AUSTRAL
LOT 15 29 DEW STREET
AUSTRAL



DRAWING TITLE:
GENERAL NOTES

NORTH:

LOT NO:	DATE:	SCALE:	DRAWING No:	REV:
15	7-09-2026	1 : 2	CDC.02A	6
DRAWN BY:	CHECKED BY:	CLIENT NAME:	ISSUED BY:	
AS	RH	Abigail & Bhikinkosi Thembinkosi Madondo		
DRAFTED BY:	SL			

CDC ISSUE


- TERMITE SHEET EXTENDS THROUGH THE ENTIRE MASONRY LEAF AND IS **VISIBLE AT THE FINISHED FACE OF THE WALL.**

 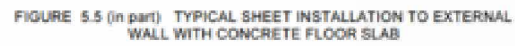

DAMP-PROOF COURSE (DPC) TO EXTENDS THROUGH THE ENTIRE MASONRY LEAF AND NEED TO BE VISIBLE AT THE FINISHED FACE OF THE WALL FROM OUTSIDE



- SURFACE DRAIN & OVERFLOW TO BALCONY

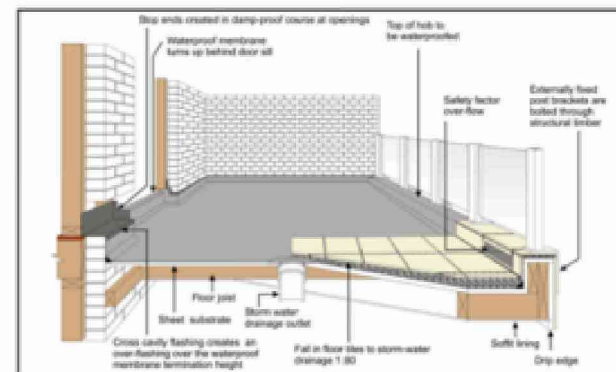


THIS DRAWING IS THE EXCLUSIVE PROPERTY OF THE DEVELOPER & THE REPRODUCTION OF ANY PART WITHOUT THE PRIOR WRITTEN CONSENT OF THE DEVELOPER IS A VIOLATION OF APPLICABLE LAWS. IN NO EVENT SHALL THE DEVELOPER BE HELD LIABLE FOR SPECIAL, COLLATERAL, INCIDENTAL OR CONSEQUENTIAL LIABILITY IN CONNECTION WITH THE USE OF THIS DIGITAL DATA ONCE RELEASED FROM THE DEVELOPER'S OFFICE. THIS DRAWING IS TO BE READ & UNDERSTOOD IN CONJUNCTION WITH THE STRUCTURAL, MECHANICAL, ELECTRICAL & / OR ANY OTHER CONSULTANT DOCUMENTATION AS MAY BE APPLICABLE TO THE PROJECT PRIOR TO THE START OF ANY WORKS AND FOR ITS DURATION.


NORTH:

LOT NO: 15	DATE: 7-09-2026	SCALE:	DRAWING No:	REV: 6
DRAWN BY: AS	CHECKED BY: RH	1 : 2	CDC.2B	ISSUED BY:
DRAFTED BY: SL	CLIENT NAME: Abigail & Bhekinkosi Thembinkosi Madondo			

CDC ISSUE

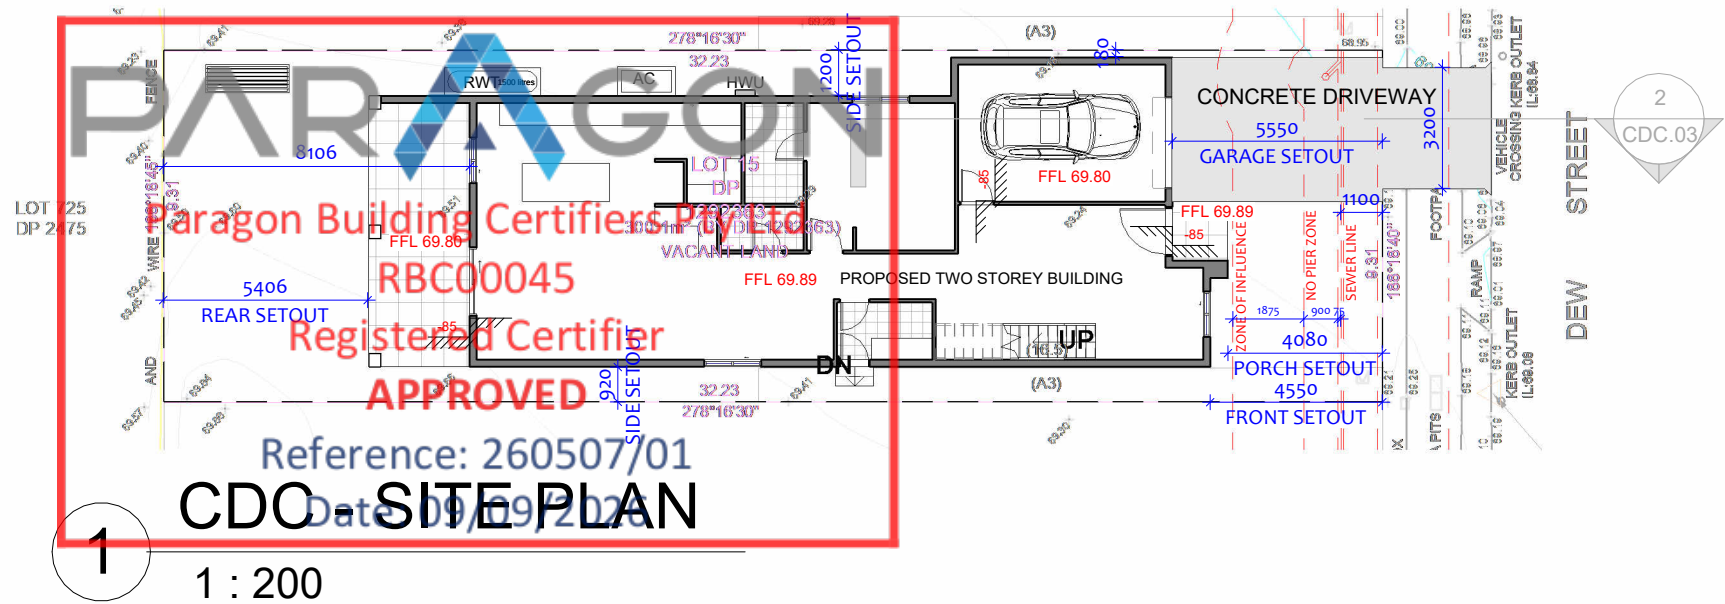

AREA SCHEDULE (RENTABLE)	
NAME	AREA (m2)
LOT AREA	300.1
GROUND FLOOR	112
FIRST FLOOR	115
GARAGE	20
STAIRSCASE VOID	11
PRIVATE OPEN SPACE	16
DRIVEWAY	21.4
FRONT LANDSCAPE	23.3
REAR LANDSCAPE	50.33

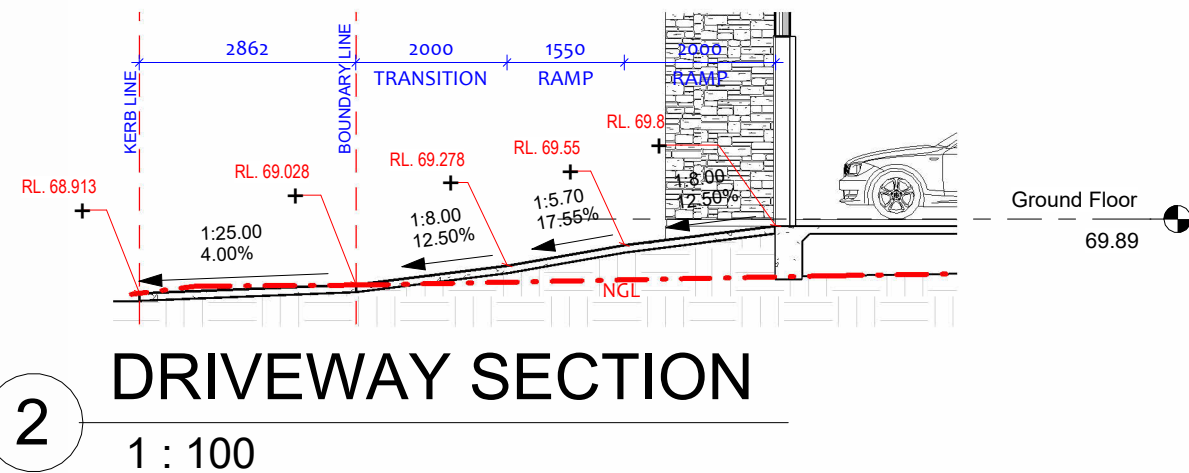

GREENFIELD HOUSING CODE COMPLIANCE TABLE

DESCRIPTION		COMPLIANCE		COMMENT
ELEMENT	CODE CONTROL	REQUIREMNT	PROPOSED	
LAND ZONE	1 GENERAL RESIDENTIAL			
LOT NO	LOT 15			
LOT AREA	300.1 m2			
LOT WIDTH	Standard Lot Min. 6m at Building Line facing primary road	6.0m	9.31 m	YES
HEIGHT	MAX. Height	8.5m	7.8m (MAX.)	YES
FRONT SETBACK	FRONT SET BACK (Min. Setback from Primary Road) For 300-350 sqm. Lot	4.5 m	4.5m	YES
REAR SET BACK (MIN.)	GROUND FLOOR	3m	5.4m	YES
	FIRST FLOOR	6m	8.1 m	
SIDE SET BACK (MIN.)	GROUND FLOOR	0/0.9m	0.18/0.92m	YES
	FIRST FLOOR	1.2/0.9m	1.2/0.92m	
FLOOR SPACE RATIO (FSR)	235 sqm.	235.00m2	229 m2	YES
GROSS FLOOR AREA PLAN	GROUND FLOOR		112 m2	
	FIRST FLOOR		115 m2	
TOTAL FLOOR AREA			227 m2	
ROOF AREA			176 m2	
GARAGE			20m2	
PRIVATE OPEN SPACE	<=10m Lot width	16m2	16 m2	YES
LANDSCAPE AREA	15 % of TOTAL LAND AREA	45.051 m2	73.63 m2	YES

(A3) EASEMENT FOR ACCESS, MAINTENANCE & REPAIRS 0.9 WIDE

REV	DATE	DESCRIPTION	BY
6	20-08-2025	CDC ISSUE	

RUBY HOMES

THIS DRAWING IS THE EXCLUSIVE PROPERTY OF THE DEVELOPER & THE REPRODUCTION OF ANY PART WITHOUT THE PRIOR WRITTEN CONSENT OF THE DEVELOPER IS A VIOLATION OF APPLICABLE LAWS. IN NO EVENT SHALL THE DEVELOPER BE HELD LIABLE FOR SPECIAL COLLATERAL, INCIDENTAL OR CONSEQUENTIAL LIABILITY IN CONNECTION WITH THE USE OF THIS DIGITAL DATA ONCE RELEASED FROM THE DEVELOPER'S OFFICE. THIS DRAWING IS TO BE READ & UNDERSTOOD IN CONJUNCTION WITH THE STRUCTURAL, MECHANICAL, ELECTRICAL & / OR ANY OTHER CONSULTANT'S DOCUMENTATION AS MAY BE APPLICABLE TO THE PROJECT PRIOR TO THE START OF ANY WORKS AND FOR ITS DURATION.

PROJECT:
29 DEW STREET AUSTRAL
LOT 15 29 DEW STREET AUSTRAL

DRAWING TITLE:
LOCATION PLAN AND SITE PLAN







LOT NO:	15	DATE:	7-09-2026	SCALE:	As indicated	DRAWING No:	CDC.03	REV:	6
DRAWN BY:	AS	CHECKED BY:	RH					ISSUED BY:	
DRAFTED BY:	SL	CLIENT NAME:	Abigail & Bhinkosi Thembinkosi Madondo						

CDC ISSUE



SD 5-7 STABILISED SITE ACCESS

- 1) STRIP TOPSOIL AND LEVEL SITE.
- 2) COMPACT SUBGRADE.
- 3) COVER AREA WITH GEOTEXILE.
- 4) CONSTRUCT 200 mm THICK PAD OVER GEOTEXILE USING ROADBASE OR 30 mm AGGREGATE. Min 15 m LONG OR TO BUILDING ALIGNMENT. Min 3 m WIDE.
- 5) CONSTRUCT HUMP IMMEDIATELY WITHIN BOUNDARY TO DIVERT WATER TO A SEDIMENT FENCE OR OTHER SEDIMENT TRAP.

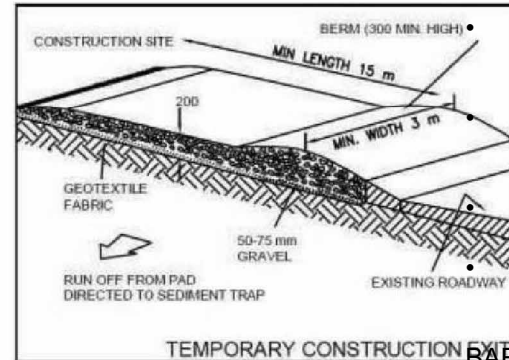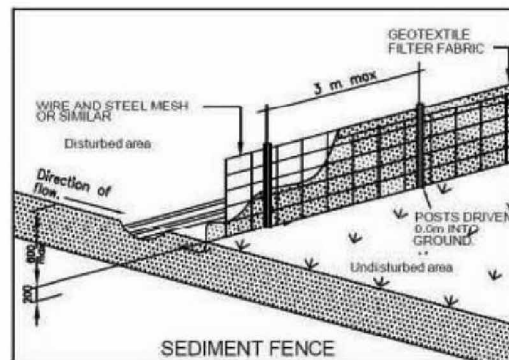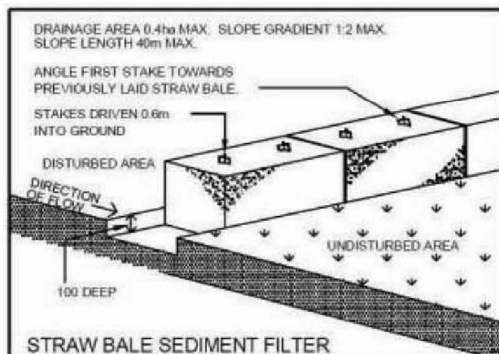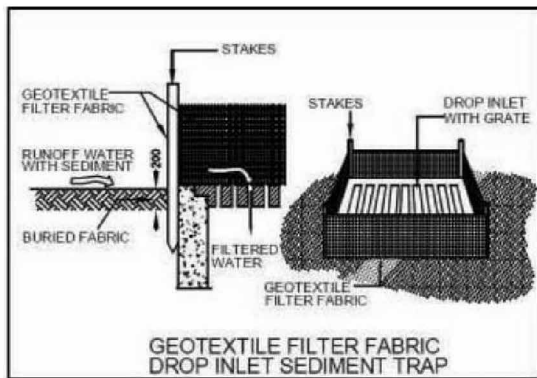

- TEMPORARY 1.8M HIGH WIRE ML FENCE WITH DUSTPROOF MESH APPLIED TO FULL HEIGHT TO BOUNDARIES AS REQUIRED
- LOCATION OF WASTE BINS
- SEDIMENT FENCE AS REQUIRED
- GRAVEL ACCESS
- SITE ACCESS AREA TO BE USED FOR WASHDOWN AREA
- FOOTPATH CLEAN AND CLEAR AT ALL TIMES
- LOCATION OF STOCKPILE MATERIAL
- MATERIAL STORAGE AREA
- TEMPORARY TOILETS
- INSTALL TEMPORARY SEDIMENT BARRIERS TO ALL INLET PITS LIKELY TO COLLECT SILT LADEN WATER, TO COUNCIL'S REQUIREMENTS.

SD 6-9 GEOTEXTILE INLET FILTER

- 1) FABRICATE A SEDIMENT BARRIER MADE FROM GEOTEXILE. REFER SD6-7 FOR DETAILS.
- 2) SUPPORT GEOTEXILE WITH MESH TIED TO POSTS AT 1 m Ctrs.
- 3) DO NOT COVER INLET WITH GEOTEXILE.

SITE WORKS NOTES

1. ORIGIN OF LEVELS PROVIDED BY SURVEYOR
2. THE BUILDER SHALL VERIFY ALL DIMENSIONS AND EXISTING LEVELS ON SITE PRIOR TO THE COMMENCEMENT OF WORK AND ANY DISCREPANCIES SHALL BE REPORTED TO THE SURVEYOR / ENGINEER.
3. TOPSOIL SHALL BE STRIPPED FROM THE CONSTRUCTION AREA AND STOCKPILED ON SITE, TO BE LATER SPREAD OR DISPOSED OFF SITE AS DIRECTED BY SUPERVISOR / ENGINEER.
4. ALL TRENCH BACKFILL MATERIAL SHALL BE COMPACTED TO THE SAME DENSITY AS THE ADJACENT MATERIAL.
5. ALL SERVICE TRENCHES UNDER VEHICULAR PAVEMENTS SHALL BE BACKFILLED WITH SAND OR APPROVED GRANULAR MATERIALS, TO THE UNDERSIDE OF THE PAVEMENT, AND COMPACTED TO 98% STANDARD MAXIMUM DRY DENSITY, IN ACCORDANCE WITH AS 1289E1.1.

SEDIMENT AND EROSION NOTES:

- THIS PLAN TO BE READ IN CONJUNCTION WITH SEDIMENT AND EROSION CONTROL DETAILS AS ATTACHED.
- THE CONTRACTOR SHALL IMPLEMENT ALL SOIL EROSION AND SEDIMENT CONTROL MEASURES AS NECESSARY AND TO THE SATISFACTION OF COUNCIL PRIOR TO THE COMMENCEMENT AND DURING CONSTRUCTION. NO DISTURBANCE TO THE SITE SHALL BE PERMITTED OTHER THAN IN THE IMMEDIATE AREA OF THE WORK AND NO MATERIAL SHALL BE REMOVED FROM THE SITE WITHOUT COUNCIL'S APPROVAL. ALL SEDIMENT AND EROSION CONTROL DEVICES TO BE INSTALLED AND MAINTAINED IN ACCORDANCE WITH STANDARDS OUTLINED IN NSW DEPARTMENT OF HOUSING "MANAGING URBAN STORMWATER-SOILS AND CONSTRUCTIONS".
- TOPSOIL SHALL BE STRIPPED AND STOCKPILED OUTSIDE HAZARD AREAS SUCH AS DRAINAGE LINES. THIS TOP SOIL IS TO BE RESPIRED LATER ON AREAS TO BE REVEGETATED AND STABILISED ONLY. (I.E ALL FOOTPATHS, BATTERS, SITE REGARDING AREAS, BASINS AND CATCH DRAINS). TOPSOIL SHALL NOT BE RESPIRED ON ANY OTHER AREAS UNLESS SPECIALLY INSTRUCTED BY THE SUPERINTENDENT. IF THEY ARE TO REMAIN FOR LONGER THAN ONE MONTH STOCKPILES SHALL BE PROTECTED FROM EROSION BY COVERING THEM WITH A MULCH AND HYDROSEEDING AND, IF NECESSARY, BY LOCATING BANKS OR DRAINS DOWNSTREAM OF A STOCKPILE TO RETARD SILT LADEN RUNOFF.
- THE CONTRACTOR SHALL REGULARLY MAINTAIN ALL SEDIMENT AND EROSION CONTROL DEVICES AND REMOVE ACCUMULATED SILT FROM SUCH DEVICES SUCH THAT MORE THAN 60% OF THEIR CAPACITY NOT LOST. ALL THE SILTS TO BE PLACED OUTSIDE THE LIMIT OF WORKS. THE PERIOD FOR MAINTAINING THESE DEVICES SHALL BE AT LEAST UNTIL ALL DISTURBED AREAS ARE REVEGETATED AND FURTHER AS MAY BE DIRECTED BY THE SUPERINTENDENT OR COUNCIL.
- LAY TURF STRIP (MIN 300 mm WIDE) ON 100 mm TOPSOIL WITH 1.0 m LONG RETURNS EVERY 6.0m BEHIND ALL KERB AT THE TOP OF ALL BATTERS AND AROUND STRUCTURES IMMEDIATELY AFTER BACKFILLING OR FORMATION.
- THE CONTRACTOR SHALL GRASS SEED ALL DISTURBED AREAS WITH AN APPROVED MIX AS SHOWN AS PRACTICABLE AFTER COMPLETION OF EARTHWORKS AND REGRADING.
- VEHICULAR TRAFFIC SHALL BE CONTROLLED DURING CONSTRUCTION CONFINING ACCESS WHERE POSSIBLE TO NOMINATED STABILISED ACCESS POINTS.
- WHEN ANY DEVICES ARE TO BE HANDED OVER TO COUNCIL, THEY SHALL BE IN CLEAN AND STABLE CONDITION.
- THE CONTRACTOR SHALL IMPLEMENT DUST CONTROL BY REGULAR WETTING DOWN (BUT NOT SATURATING) DISTURBED AREA.
- PROVIDE AND MAINTAIN SILT TRAPS AROUND ALL SURFACE INLET PITS UNTIL CATCHMENT IS REVEGETATED OR PAVED.
- REVEGETATE ALL TRENCHES IMMEDIATELY UPON COMPLETION OF BACKFILLING.
- ALL DRAINAGE PIPE INLETS TO BE CAPPED UNTIL:
 - A) DOWNPIPES CONNECTED
 - B) PITS CONSTRUCTED & PROTECTED WITH SILT

CDC ISSUE


REV	DATE	DESCRIPTION	BY
6	20-08-2025	CDC ISSUE	

RUBY HOMES

THIS DRAWING IS THE EXCLUSIVE PROPERTY OF THE DEVELOPER & THE REPRODUCTION OF ANY PART WITHOUT THE PRIOR WRITTEN CONSENT OF THE DEVELOPER IS A VIOLATION OF APPLICABLE LAWS. IN NO EVENT SHALL THE DEVELOPER BE HELD LIABLE FOR SPECIAL COLLATERAL, INCIDENTAL OR CONSEQUENTIAL LIABILITY IN CONNECTION WITH THE USE OF THIS DIGITAL DATA ONCE RELEASED FROM THE DEVELOPER'S OFFICE. THIS DRAWING IS TO BE READ & UNDERSTOOD IN CONJUNCTION WITH THE STRUCTURAL, MECHANICAL, ELECTRICAL & / OR ANY OTHER CONSULTANT'S DOCUMENTATION AS MAY BE APPLICABLE TO THE PROJECT PRIOR TO THE START OF ANY WORKS AND FOR ITS DURATION.

PROJECT:
**29 DEW STREET
AUSTRAL**
LOT 15 29 DEW STREET
AUSTRAL

DRAWING TITLE:
**SITE ANALYSIS
AND SEDIMENT
CONTROL**

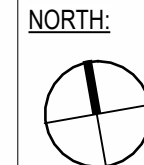

LOT NO: 15	DATE: 7-09-2026	SCALE: As indicated	DRAWING No: CDC.04	REV: 6
DRAWN BY: AS	CHECKED BY: RH	CLIENT NAME: Abigail & Bhikinkosi Thembinkosi Madondo	ISSUED BY:	

WATERPROOFING WORK TO BE AS PER PART 10.2 OF THE ABCB HOUSING PROVISIONS STANDARD 2022

Figure 11.2.2a Measurement of slope relationship — Plan view — Stair with 2 flights


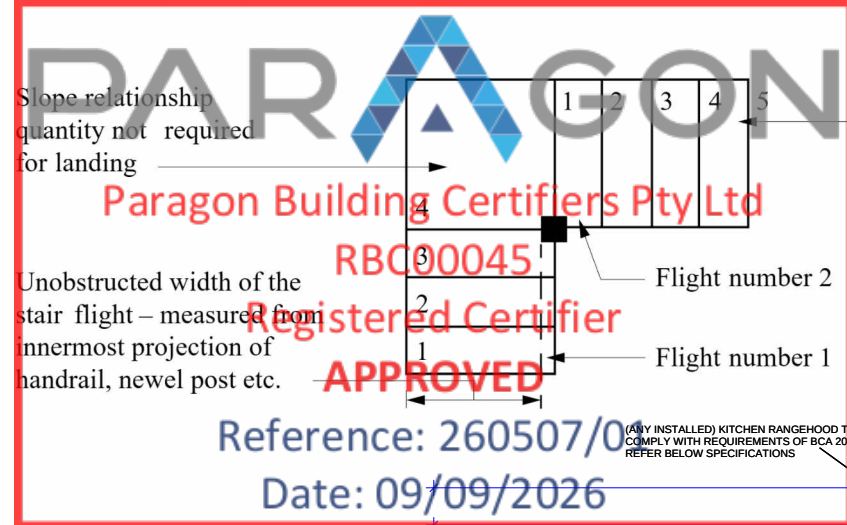


Table 11.2.2a Riser and going dimensions (mm)

Stair type	Riser (R) (see Figure 11.2.2f)		Going (G) (see Figure 11.2.2f)		Slope relationship (2R+G)	
	Max	Min	Max	Min	Max	Min
Stairs (other than spiral)	190	115	355	240	700	550
Spiral	220	140	370	210	680	590

Table Notes

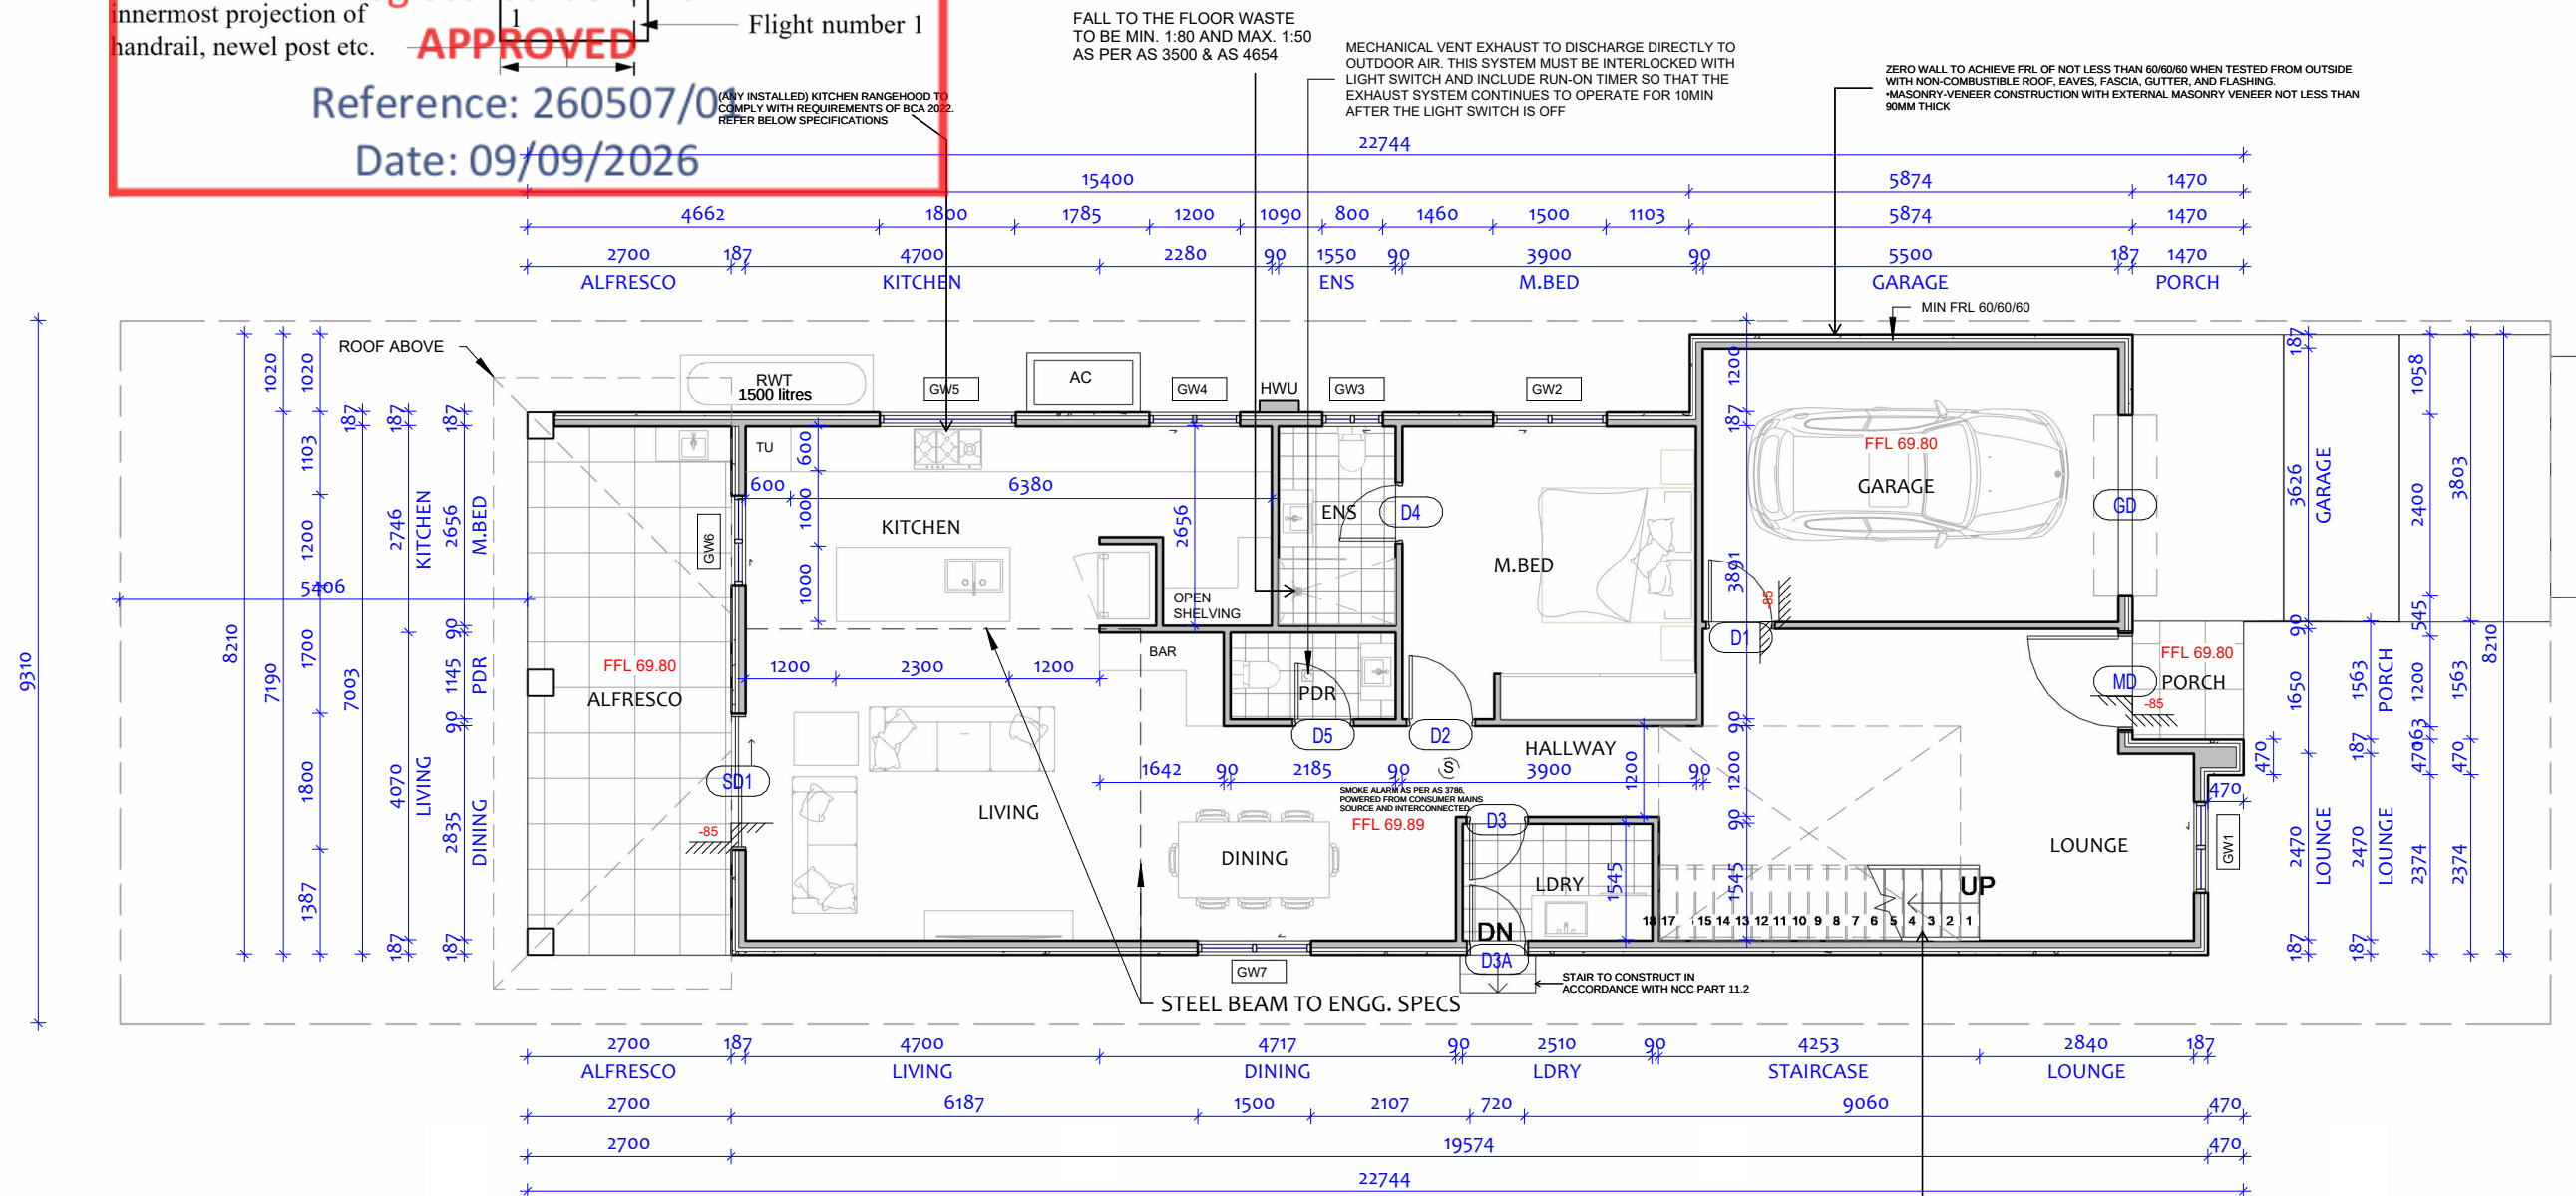

1

Ground Floor

1 : 100

NOTE: PLEASE REFER TO TENDER FOR ALL INCLUSIONS.

REV	DATE	DESCRIPTION	BY
6	20-08-2025	CDC ISSUE	
2	24-07-2025	Revision 2	
1	16-07-2025	Concept Issue	

RUBY HOMES

THIS DRAWING IS THE EXCLUSIVE PROPERTY OF THE DEVELOPER & THE REPRODUCTION OF ANY PART WITHOUT THE PRIOR WRITTEN CONSENT OF THE DEVELOPER IS A VIOLATION OF APPLICABLE LAWS. IN NO EVENT SHALL THE DEVELOPER BE HELD LIABLE FOR SPECIAL COLLATERAL, INCIDENTAL OR CONSEQUENTIAL LIABILITY IN CONNECTION WITH THE USE OF THIS DIGITAL DATA ONCE RELEASED FROM THE DEVELOPER'S OFFICE. THIS DRAWING IS TO BE READ & UNDERSTOOD IN CONJUNCTION WITH THE STRUCTURAL, MECHANICAL, ELECTRICAL & / OR ANY OTHER CONSULTANT'S DOCUMENTATION AS MAY BE APPLICABLE TO THE PROJECT PRIOR TO THE START OF ANY WORKS AND FOR ITS DURATION.

PROJECT:
29 DEW STREET AUSTRAL
LOT 15 29 DEW STREET AUSTRAL

DRAWING TITLE:
GROUND FLOOR PLAN



LOT NO:	DATE:	SCALE:	DRAWING No:	REV:
15	7-09-2026	1 : 100	CDC.05	6
DRAWN BY:	CHECKED BY:	DRAFTED BY:	CLIENT NAME:	ISSUED BY:
AS	RH	SL	Abigail & Bhinkosi Thembinkosi Madondo	


CDC ISSUE

WATERPROOFING WORK TO BE AS PER PART 10.2 OF THE ABCB HOUSING PROVISIONS STANDARD 2022


Figure 11.3.4a Barrier construction



Figure 11.3.4b Measuring heights for barriers and handrails and where transition zones are allowed

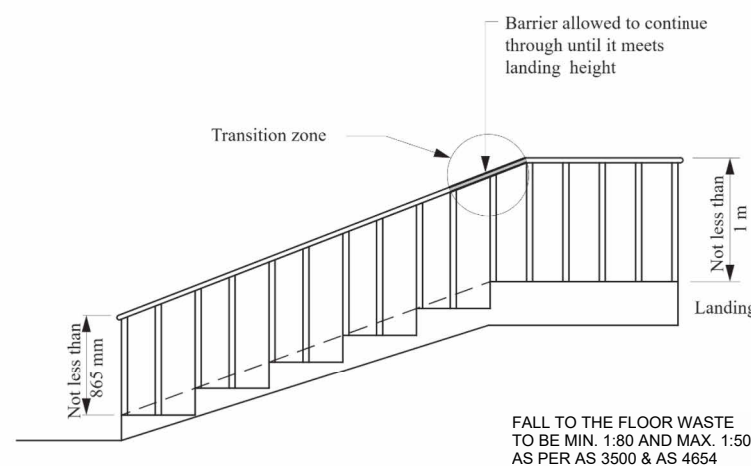

IMPORTANT NOTES:
ALL DIMENSIONS AND NOTES ON ALL PLANS MUST BE CHECKED AND VERIFIED BY BUILDERS AND OWNER PRIOR TO COMMENCEMENT OF ANY BUILDING WORKS. TO CLARIFY AND CONFIRM WITH CONSTRUCTION COMPANY FOR DISCREPANCIES ON ALL DOCUMENTS AND PLANS PROVIDED FOR CONSTRUCTION. ANY WORK INDICATED ON THE PLAN BUT NOT IN THE SPECIFICATION BUT WHICH IS NECESSARY AS PART OF THE CONTRACT. VARIATION TO PLANS, SPECIFICATIONS MAY NOT BE MADE WITHOUT THE WRITTEN CONSENT OF OWNER. IT IS THE RESPONSIBILITY OF THE BUILDER/END USER TO VERIFY PLANS AND SPECIFICATIONS AS TO THEIR ACCURACY AND COMPLY CURRENT BCA AND AUSTRALIAN STANDARDS. WINDOWS TO COMPLY WITH 3.9.3.5 OF THE BCA.

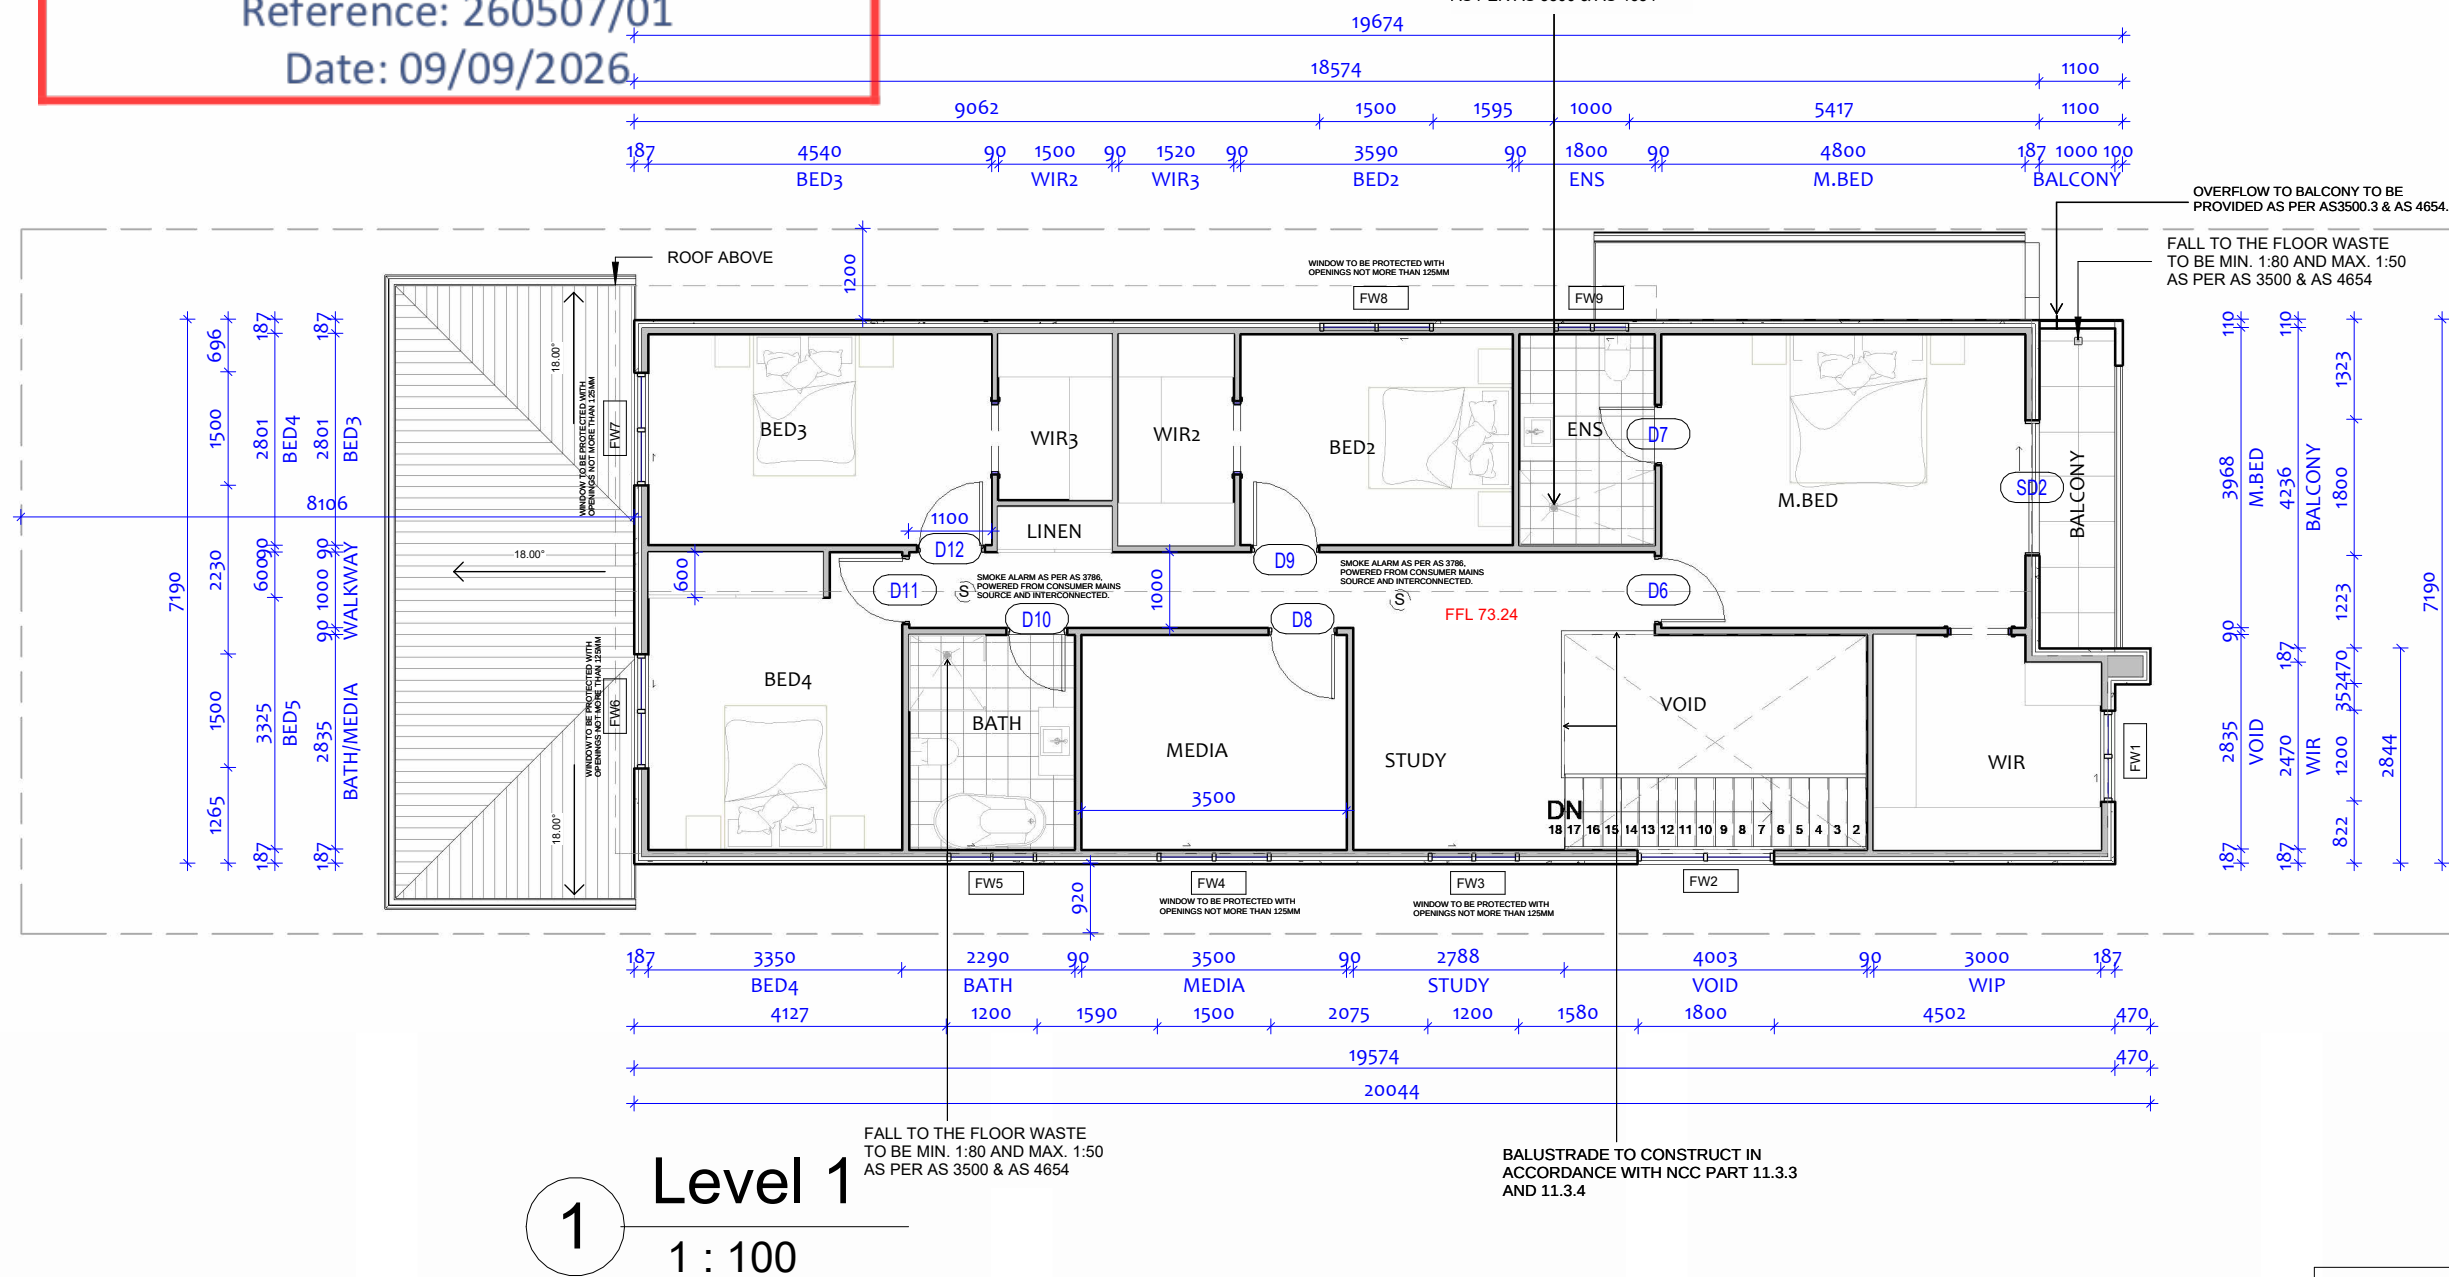

NOTE: PLEASE REFER TO TENDER FOR ALL INCLUSIONS.


REV	DATE	DESCRIPTION	BY
6	20-08-2025	CDC ISSUE	
2	24-07-2025	Revision 2	
1	16-07-2025	Concept Issue	

RUBY HOMES

THIS DRAWING IS THE EXCLUSIVE PROPERTY OF THE DEVELOPER & THE REPRODUCTION OF ANY PART WITHOUT THE PRIOR WRITTEN CONSENT OF THE DEVELOPER IS A VIOLATION OF APPLICABLE LAWS. IN NO EVENT SHALL THE DEVELOPER BE HELD LIABLE FOR SPECIAL COLLATERAL, INCIDENTAL OR CONSEQUENTIAL LIABILITY IN CONNECTION WITH THE USE OF THIS DIGITAL DATA ONCE RELEASED FROM THE DEVELOPER'S OFFICE. THIS DRAWING IS TO BE READ & UNDERSTOOD IN CONJUNCTION WITH THE STRUCTURAL, MECHANICAL, ELECTRICAL & / OR ANY OTHER CONSULTANT'S DOCUMENTATION AS MAY BE APPLICABLE TO THE PROJECT PRIOR TO THE START OF ANY WORKS AND FOR ITS DURATION.


PROJECT:
29 DEW STREET
AUSTRAL
LOT 15 29 DEW STREET
AUSTRAL

DRAWING TITLE:
FIRST FLOOR
LEVEL

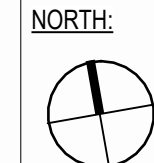

LOT NO:	DATE:	SCALE:	DRAWING No:	REV:
15	7-09-2026	1 : 100	CDC.06	6
DRAWN BY:	CHECKED BY:	CLIENT NAME:	ISSUED BY:	
AS	RH	Abigail & Bhinkosi Thembinkosi Madondo		

CDC ISSUE


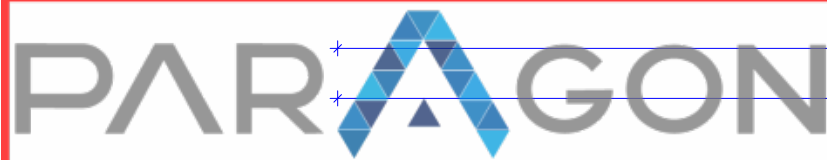


Paragon Building Certifiers Pty Ltd

RBC00045

Registered Certifier
APPROVED

Reference: 260507/01
Date: 09/09/2026

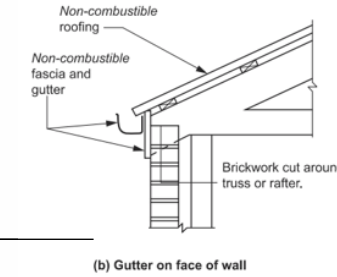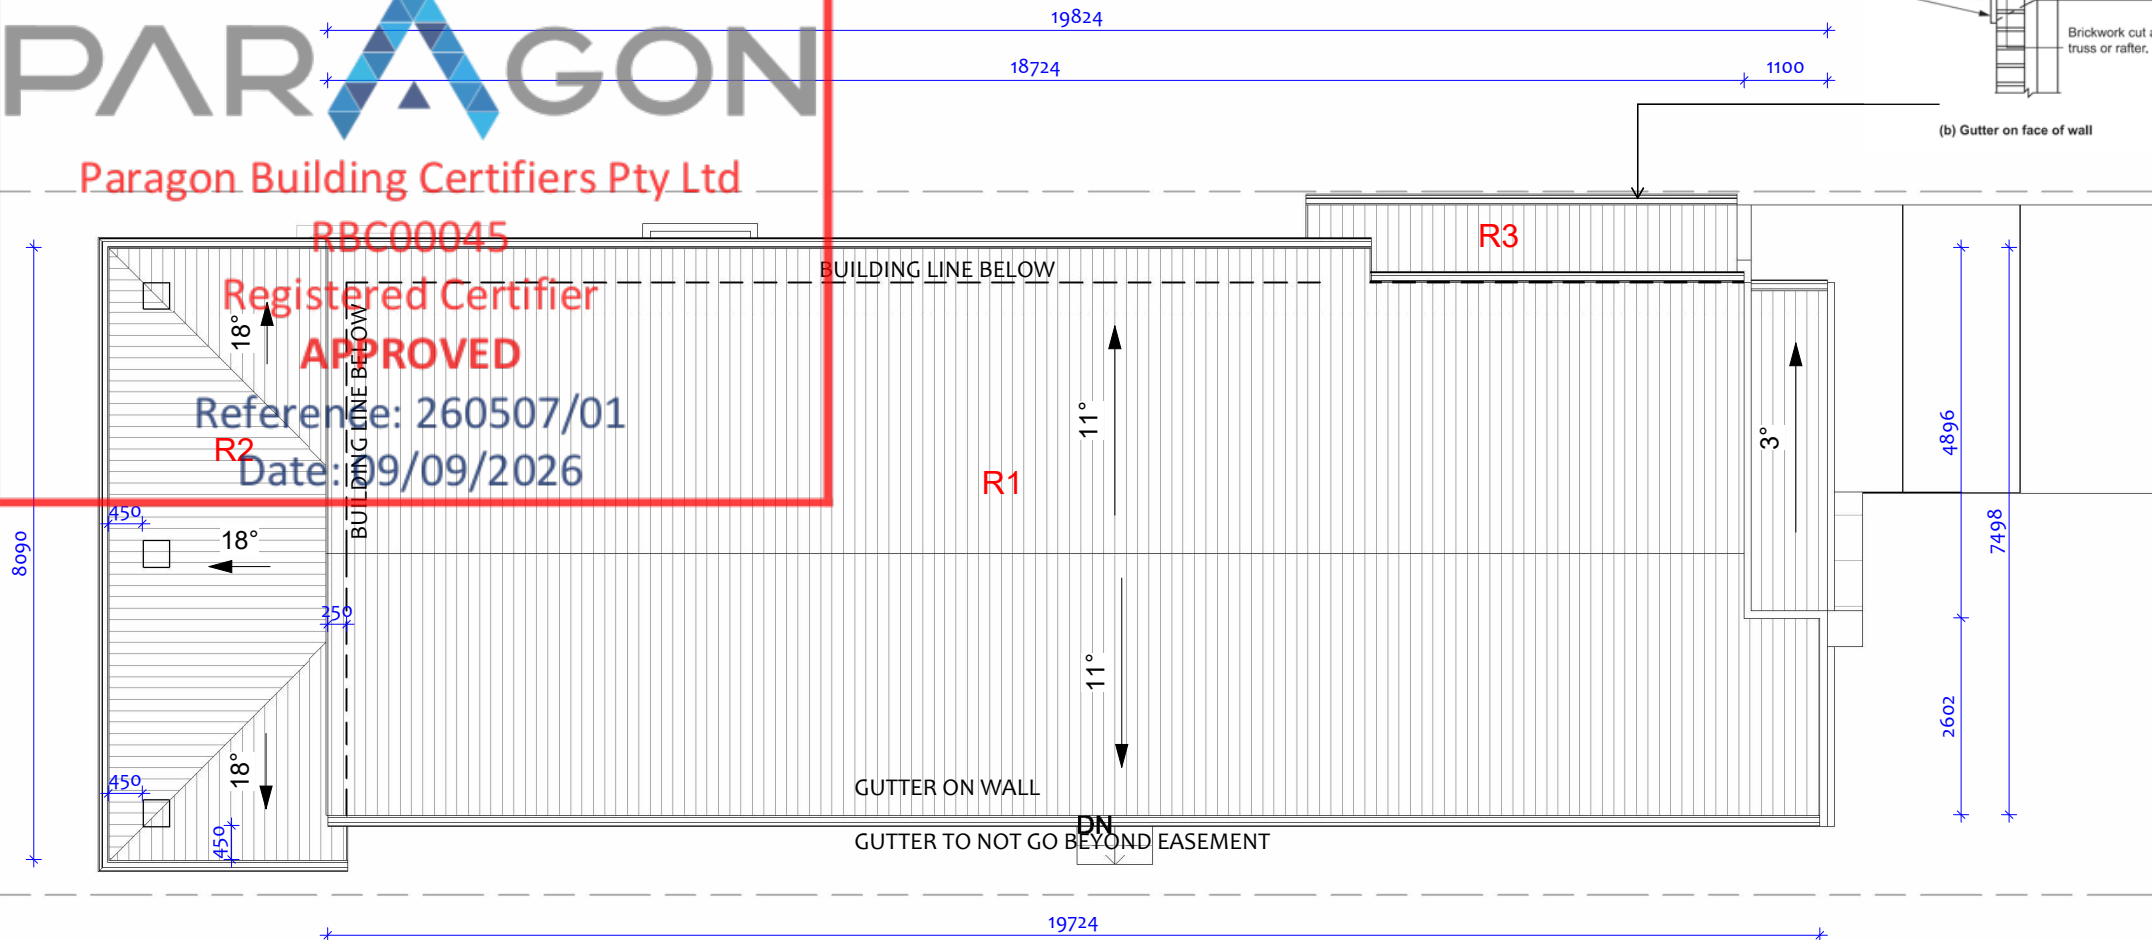

IMPORTANT NOTES:
ALL DIMENSIONS AND NOTES ON ALL PLANS MUST BE CHECKED AND VERIFIED BY BUILDERS AND OWNER PRIOR TO COMMENCEMENT OF ANY BUILDING WORKS. TO CLARIFY AND CONFIRM WITH CONSTRUCTION COMPANY FOR DISCREPANCIES ON ALL DOCUMENTS AND PLANS PROVIDED FOR CONSTRUCTION. ANY WORK INDICATED ON THE PLAN BUT NOT IN THE SPECIFICATION BUT WHICH IS NECESSARY AS PART OF THE CONTRACT, VARIATION TO PLANS, SPECIFICATIONS MAY NOT BE MADE WITHOUT THE WRITTEN CONSENT OF OWNER. IT IS THE RESPONSIBILITY OF THE BUILDER/END USER TO VERIFY PLANS AND SPECIFICATIONS AS TO THEIR ACCURACY AND COMPLY CURRENT BCA AND AUSTRALIAN STANDARDS. WINDOWS TO COMPLY WITH 3.9.3.5 OF THE BCA.

ABCB HOUSING PROVISIONS STANDARD 2022

10.8.3 VENTILATION OF ROOF SPACES

1. IN CLIMATE ZONES 6, 7 AND 8, A ROOF MUST HAVE A ROOF SPACE THAT
- (A) IS LOCATED
- (I) IMMEDIATELY ABOVE THE PRIMARY INSULATION LAYER, OR
 - (II) IMMEDIATELY ABOVE SARKING WITH A VAPOUR PERMEANCE OF NOT LESS THAN 1.14 µG/N.S, WHICH IS IMMEDIATELY ABOVE THE PRIMARY INSULATION LAYER, OR
 - (III) IMMEDIATELY ABOVE CEILING INSULATION THAT MEETS THE REQUIREMENTS OF 13.2.3(3) AND 13.2.3(4); AND
- (B) HAS A HEIGHT OF NOT LESS THAN 20MM; AND
- (C) IS EITHER
- (I) VENTILATED TO OUTDOOR AIR THROUGH EVENLY DISTRIBUTED OPENINGS IN ACCORDANCE WITH TABLE 10.8.3; OR
 - (II) LOCATED IMMEDIATELY UNDERNEATH THE ROOF TILES OF A UNSARKED TILED ROOF.

1 ROOF PLAN

1 : 100

Figure 7.2.3: Minimum pitch requirements for metal roofing profiles

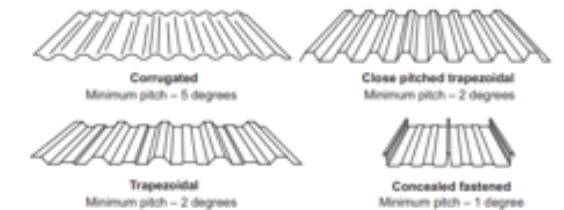


Figure 10.8.3 (explanatory): Example of roof space with low level ventilation

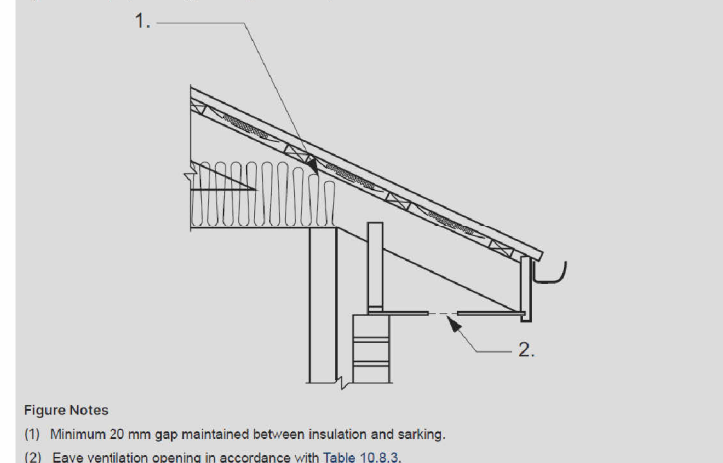


Figure Notes
(1) Minimum 20 mm gap maintained between insulation and sarking.
(2) Eave ventilation opening in accordance with Table 10.8.3.

Table 10.8.3: Roof space ventilation requirements

Roof pitch	Ventilation openings
< 10°	25,000 mm²/m provided at each of two opposing ends
≥ 10° and < 15°	25,000 mm²/m provided at the eaves and 5,000 mm²/m at high level
≥ 15° and < 75°	7,000 mm²/m provided at the eaves and 5,000 mm²/m at high level, plus an additional 18,000 mm²/m at the eaves if the roof has a cathedral ceiling

Roof Schedule			
Mark	Base Level	Area	Type
R2	Ground Ceiling	27 m²	ROOF COLORBOND
R3	Level 1	6 m²	ROOF COLORBOND
R1	CEILING LEVEL	143 m²	ROOF COLORBOND
Grand total: 3		176 m²	

CDC ISSUE

6	20-08-2025	CDC ISSUE	
5	04-07-2025	Revision 5	
4	27-06-2025	Revision 4	
3	24-06-2025	Revision 3	
2	24-07-2025	Revision 2	
1	16-07-2025	Concept Issue	
REV	DATE	DESCRIPTION	BY


THIS DRAWING IS THE EXCLUSIVE PROPERTY OF THE DEVELOPER & THE REPRODUCTION OF ANY PART WITHOUT THE PRIOR WRITTEN CONSENT OF THE DEVELOPER IS A VIOLATION OF APPLICABLE LAWS. IN NO EVENT SHALL THE DEVELOPER BE HELD LIABLE FOR SPECIAL COLLATERAL, INCIDENTAL OR CONSEQUENTIAL LIABILITY IN CONNECTION WITH THE USE OF THIS DIGITAL DATA ONCE RELEASED FROM THE DEVELOPER'S OFFICE. THIS DRAWING IS TO BE READ & UNDERSTOOD IN CONJUNCTION WITH THE STRUCTURAL, MECHANICAL, ELECTRICAL & / OR ANY OTHER CONSULTANT'S DOCUMENTATION AS MAY BE APPLICABLE TO THE PROJECT PRIOR TO THE START OF ANY WORKS AND FOR ITS DURATION.

PROJECT:
29 DEW STREET
AUSTRAL
LOT 15 29 DEW STREET
AUSTRAL


DRAWING TITLE:
ROOF PLAN



LOT NO: 15	DATE: 7-09-2026	SCALE: 1 : 100	DRAWING No: CDC.07	REV: 6
DRAWN BY: AS	CHECKED BY: RH			ISSUED BY:
DRAFTED BY: SL	CLIENT NAME: Abigail & Bhekinkosi Thembinkosi Madondo			

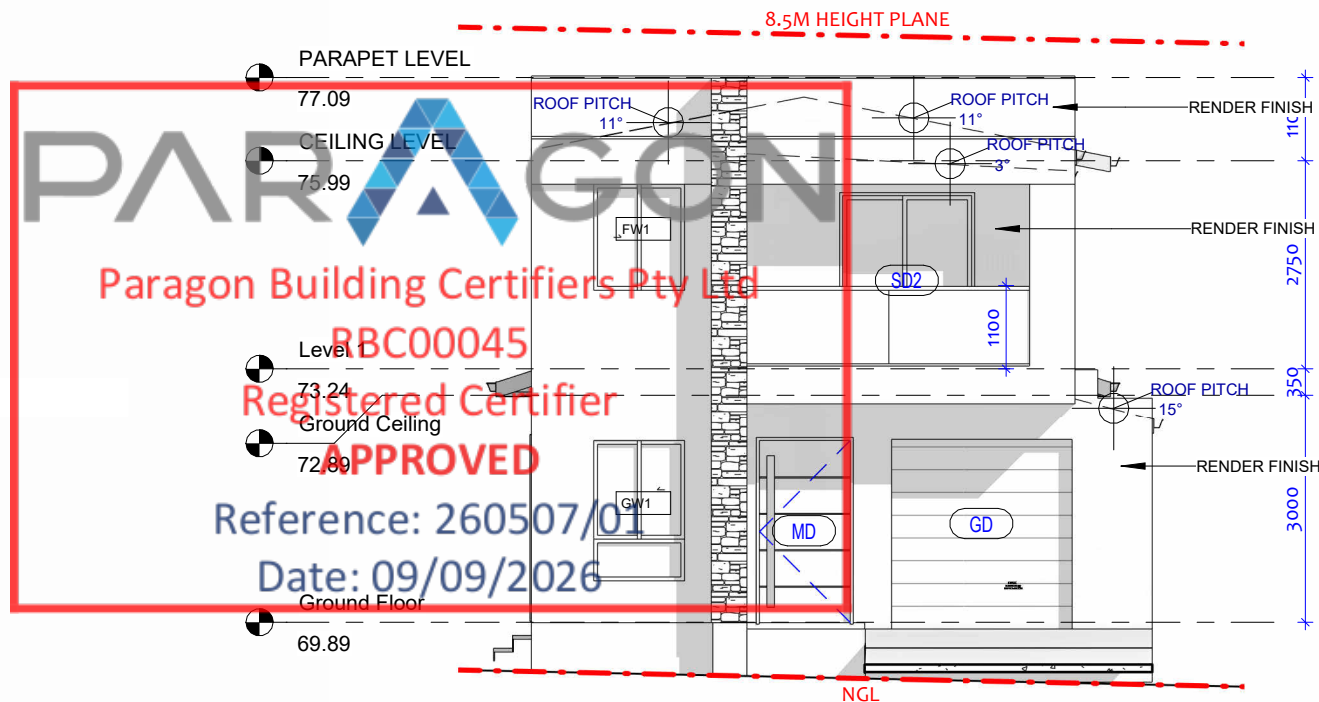

1 East Elevation
1 : 100

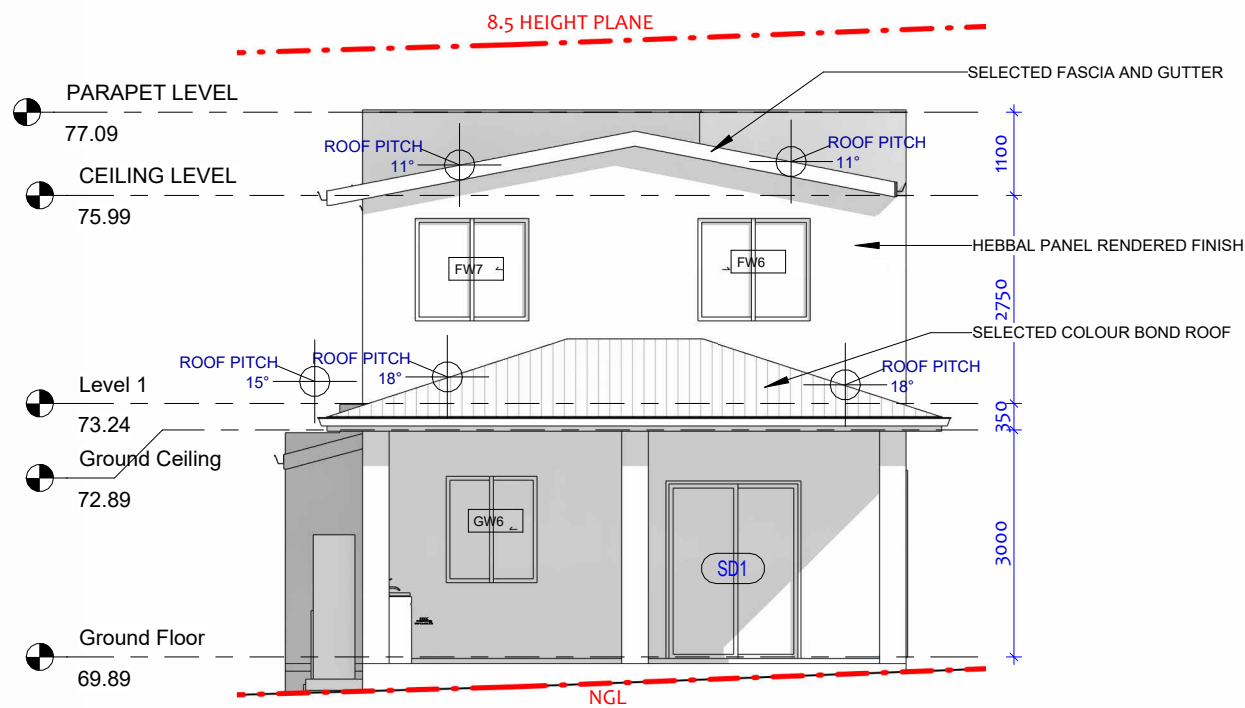

2 West Elevation
1 : 100

Window Schedule 1					
Mark	Height	Width	Sill Height	Head Height	Description

Ground Floor

GW1	1850	1200	550	2400	SLIDING
GW2	1400	1500	1000	2400	SLIDING
GW3	600	800	1000	1600	SLIDING
GW4	600	1200	950	1550	SLIDING
GW5	600	1800	950	1550	FIXED
GW6	1400	1200	1000	2400	SLIDING
GW7	1400	1500	1000	2400	SLIDING

Ground Floor: 7

Level 1

FW1	1400	1200	1050	2450	SLIDING
FW2	1500	1800	950	2450	FIXED
FW3	800	1200	1650	2450	SLIDING
FW4	800	1500	1650	2450	SLIDING
FW5	800	1200	1650	2450	SLIDING
FW6	1350	1500	1100	2450	SLIDING
FW7	1350	1500	1100	2450	SLIDING
FW8	800	1500	1650	2450	SLIDING
FW9	800	1000	1650	2450	SLIDING

Level 1: 9

Door Schedule 1				
Mark	Height	Width	Count	Description

Ground Floor

D1	2340	820	1	FLUSH DOOR
D2	2340	820	1	FLUSH DOOR
D3	2340	720	1	FLUSH DOOR
D3A	2340	720	1	FLUSH DOOR
D4	2340	720	1	FLUSH DOOR
D5	2340	720	1	FLUSH DOOR
GD	2500	2400	1	GARAGE DOOR
MD	2400	1200	1	SOLID CORE DOOR
SD1	2300	1800	1	SLIDING DOOR

Ground Floor: 9

Level 1

D6	2340	820	1	FLUSH DOOR
D7	2340	720	1	FLUSH DOOR
D8	2340	820	1	FLUSH DOOR
D9	2340	820	1	FLUSH DOOR
D10	2340	720	1	FLUSH DOOR
D11	2340	820	1	FLUSH DOOR
D12	2340	820	1	FLUSH DOOR
SD2	2300	1800	1	SLIDING DOOR

Level 1: 8

6	20-08-2025	CDC ISSUE	
5	04-07-2025	Revision 5	
4	27-06-2025	Revision 4	
3	24-06-2025	Revision 3	
2	24-07-2025	Revision 2	
1	16-07-2025	Concept Issue	
REV	DATE	DESCRIPTION	BY



RUBY
HOMES

THIS DRAWING IS THE EXCLUSIVE PROPERTY OF THE DEVELOPER & THE REPRODUCTION OF ANY PART WITHOUT THE PRIOR WRITTEN CONSENT OF THE DEVELOPER IS A VIOLATION OF APPLICABLE LAWS. IN NO EVENT SHALL THE DEVELOPER BE HELD LIABLE FOR SPECIAL COLLATERAL, INCIDENTAL OR CONSEQUENTIAL LIABILITY IN CONNECTION WITH THE USE OF THIS DIGITAL DATA ONCE RELEASED FROM THE DEVELOPER'S OFFICE. THIS DRAWING IS TO BE READ & UNDERSTOOD IN CONJUNCTION WITH THE STRUCTURAL, MECHANICAL, ELECTRICAL & / OR ANY OTHER CONSULTANT'S DOCUMENTATION AS MAY BE APPLICABLE TO THE PROJECT PRIOR TO THE START OF ANY WORKS AND FOR ITS DURATION.

PROJECT:
**29 DEW STREET
AUSTRAL**
LOT 15 29 DEW STREET
AUSTRAL

DRAWING TITLE:
ELEVATION 01

NORTH:

LOT NO:
15

DRAWN BY:
AS

DRAFTED BY:
SL

DATE:
7-09-2026

CHECKED BY:
RH

CLIENT NAME:
Abigail & Bhinkosi Thembinkosi Madondo


SCALE:
1 : 100

DRAWING No:
CDC.08


REV:
6

ISSUED BY:

CDC ISSUE

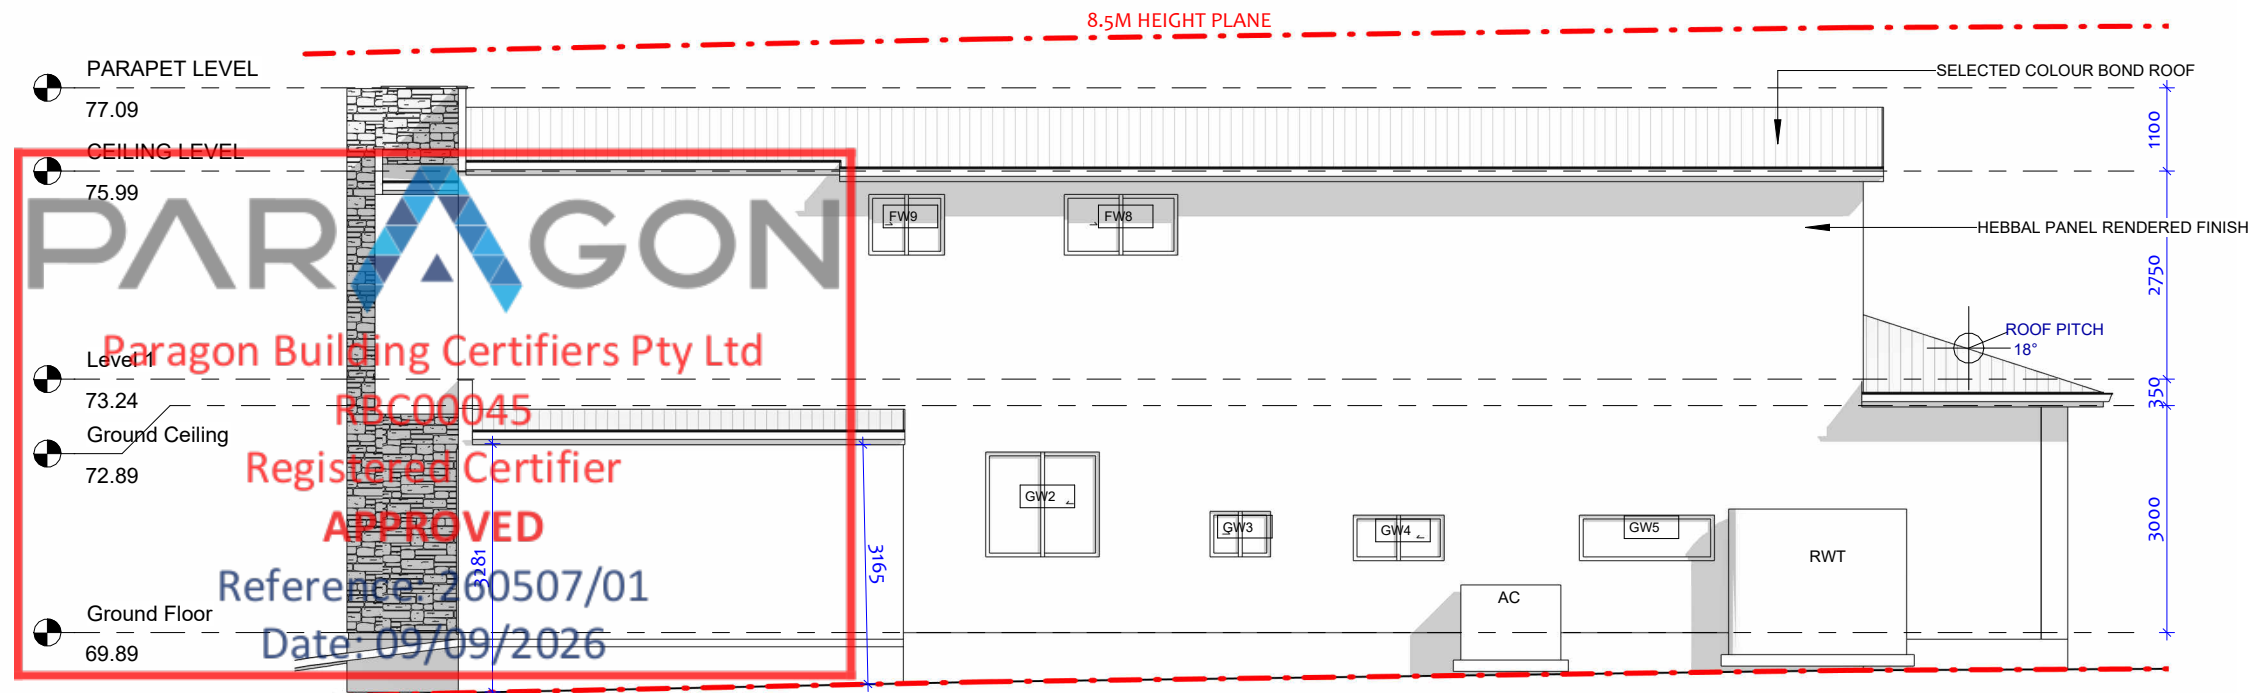

1 South Elevation
1 : 100

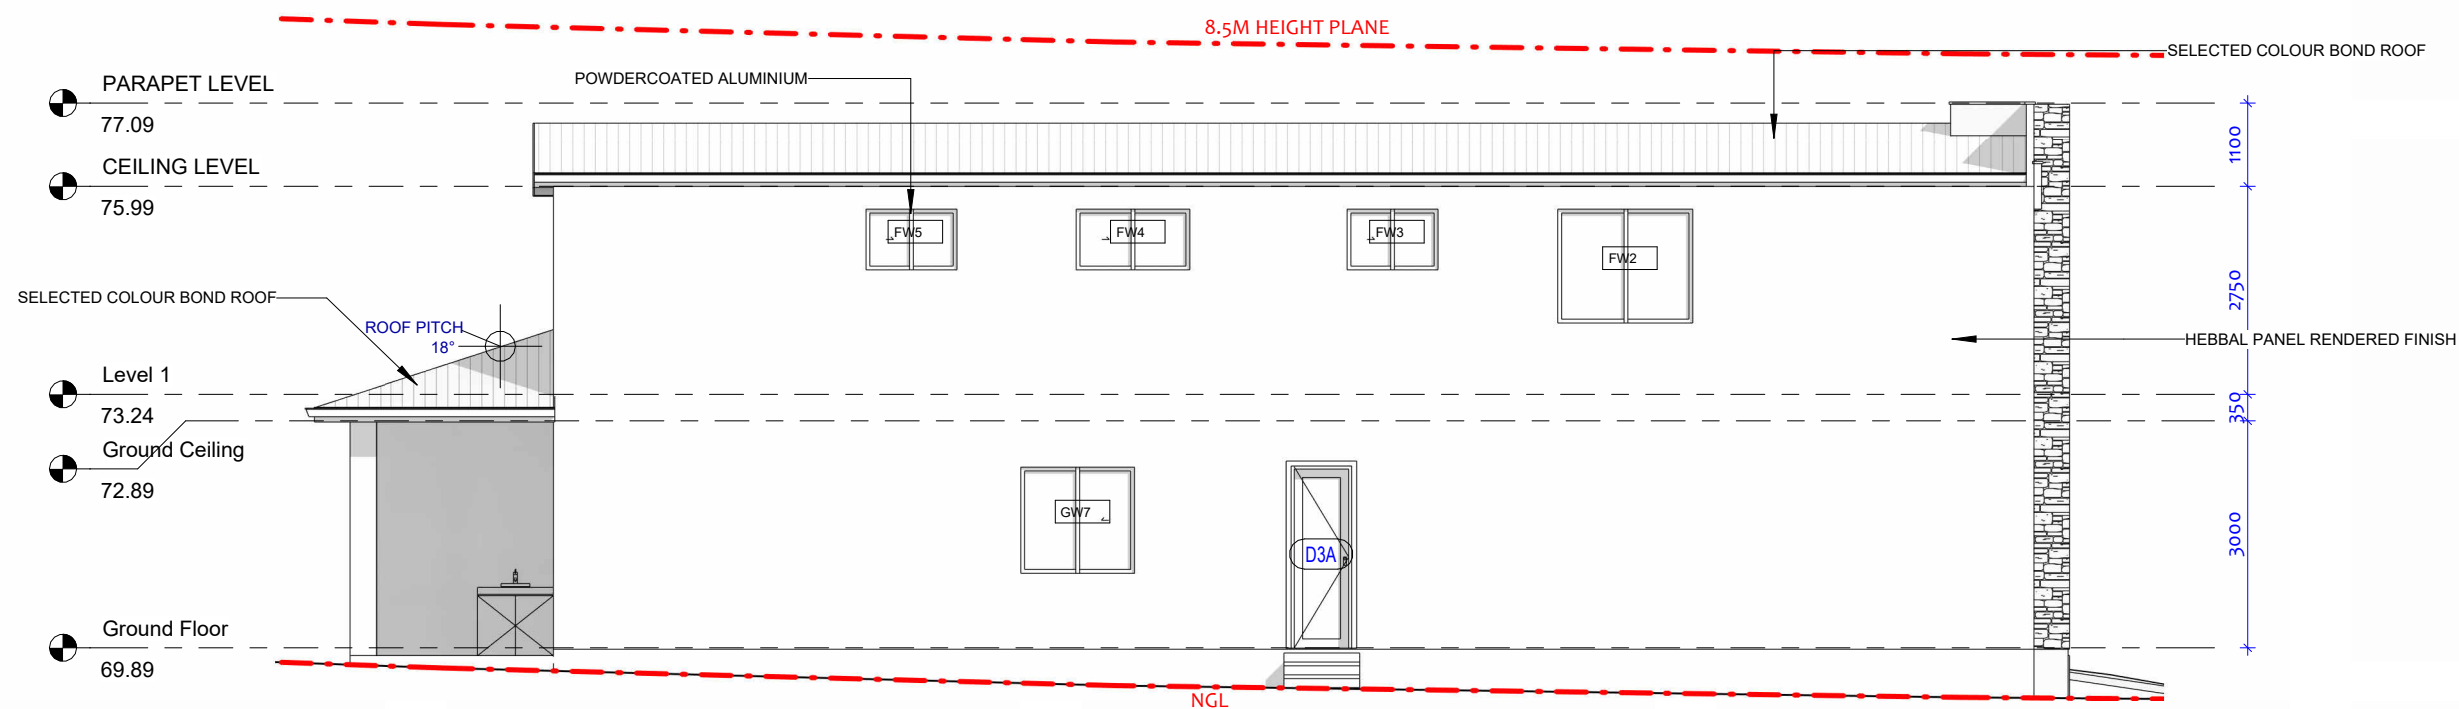

2 North Elevation
1 : 100

REV	DATE	DESCRIPTION	BY
6	20-08-2025	CDC ISSUE	
5	04-07-2025	Revision 5	
4	27-06-2025	Revision 4	
3	24-06-2025	Revision 3	
2	24-07-2025	Revision 2	
1	16-07-2025	Concept Issue	


RUBY
H O M E S

THIS DRAWING IS THE EXCLUSIVE PROPERTY OF THE DEVELOPER & THE REPRODUCTION OF ANY PART WITHOUT THE PRIOR WRITTEN CONSENT OF THE DEVELOPER IS A VIOLATION OF APPLICABLE LAWS. IN NO EVENT SHALL THE DEVELOPER BE HELD LIABLE FOR SPECIAL COLLATERAL, INCIDENTAL OR CONSEQUENTIAL LIABILITY IN CONNECTION WITH THE USE OF THIS DIGITAL DATA ONCE RELEASED FROM THE DEVELOPER'S OFFICE. THIS DRAWING IS TO BE READ & UNDERSTOOD IN CONJUNCTION WITH THE STRUCTURAL, MECHANICAL, ELECTRICAL & / OR ANY OTHER CONSULTANT'S DOCUMENTATION AS MAY BE APPLICABLE TO THE PROJECT PRIOR TO THE START OF ANY WORKS AND FOR ITS DURATION.

PROJECT:
**29 DEW STREET
AUSTRAL**
LOT 15 29 DEW STREET
AUSTRAL

DRAWING TITLE:
ELEVATION 02

NORTH:

LOT NO:
15
DRAWN BY:
AS
DRAFTED BY:
SL

DATE:
7-09-2026
CHECKED BY:
RH

SCALE:
1 : 100

CDC ISSUE

DRAWING No:
CDC.09
REV:
6
ISSUED BY:

CLIENT NAME:
Abigail & Bhengkosi Thembinkosi Madondo

PARAGON

Paragon Building Certifiers Pty Ltd


RBC00045

Registered Certifier


APPROVED

Reference: 260507/01

Date: 09/09/2026

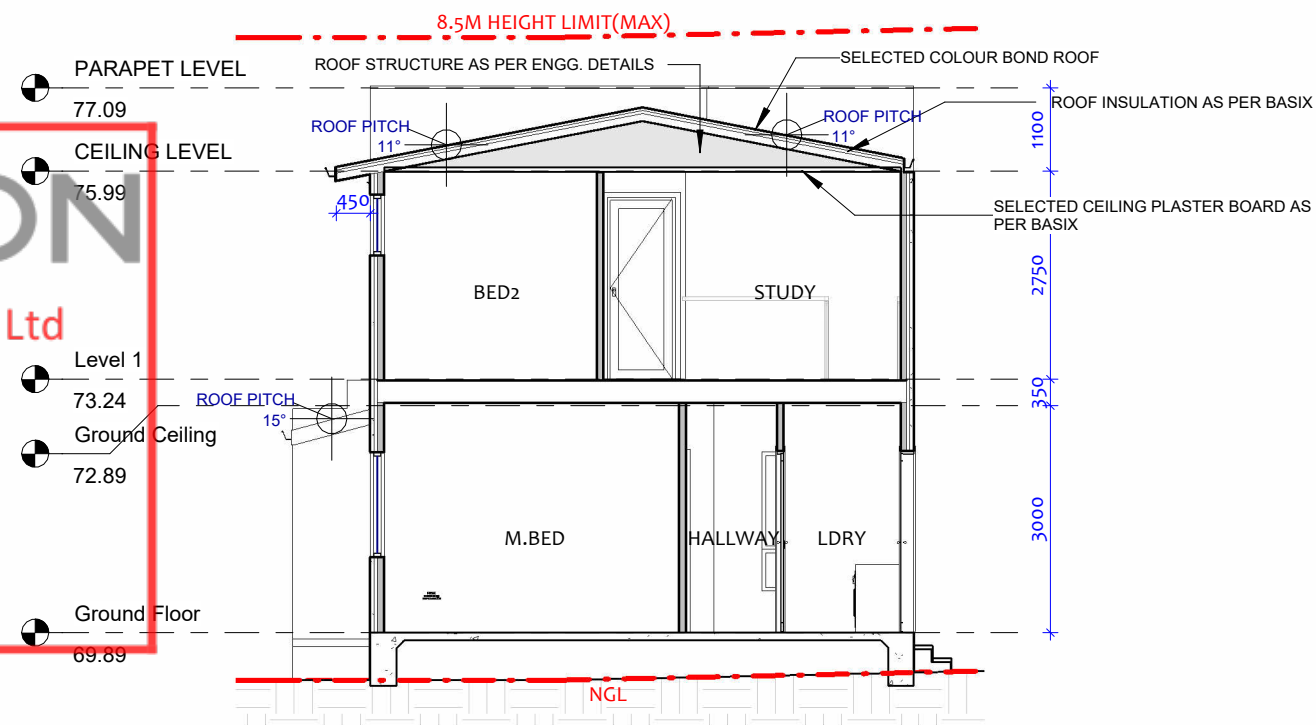

1 CROSS SECTION
1 : 100

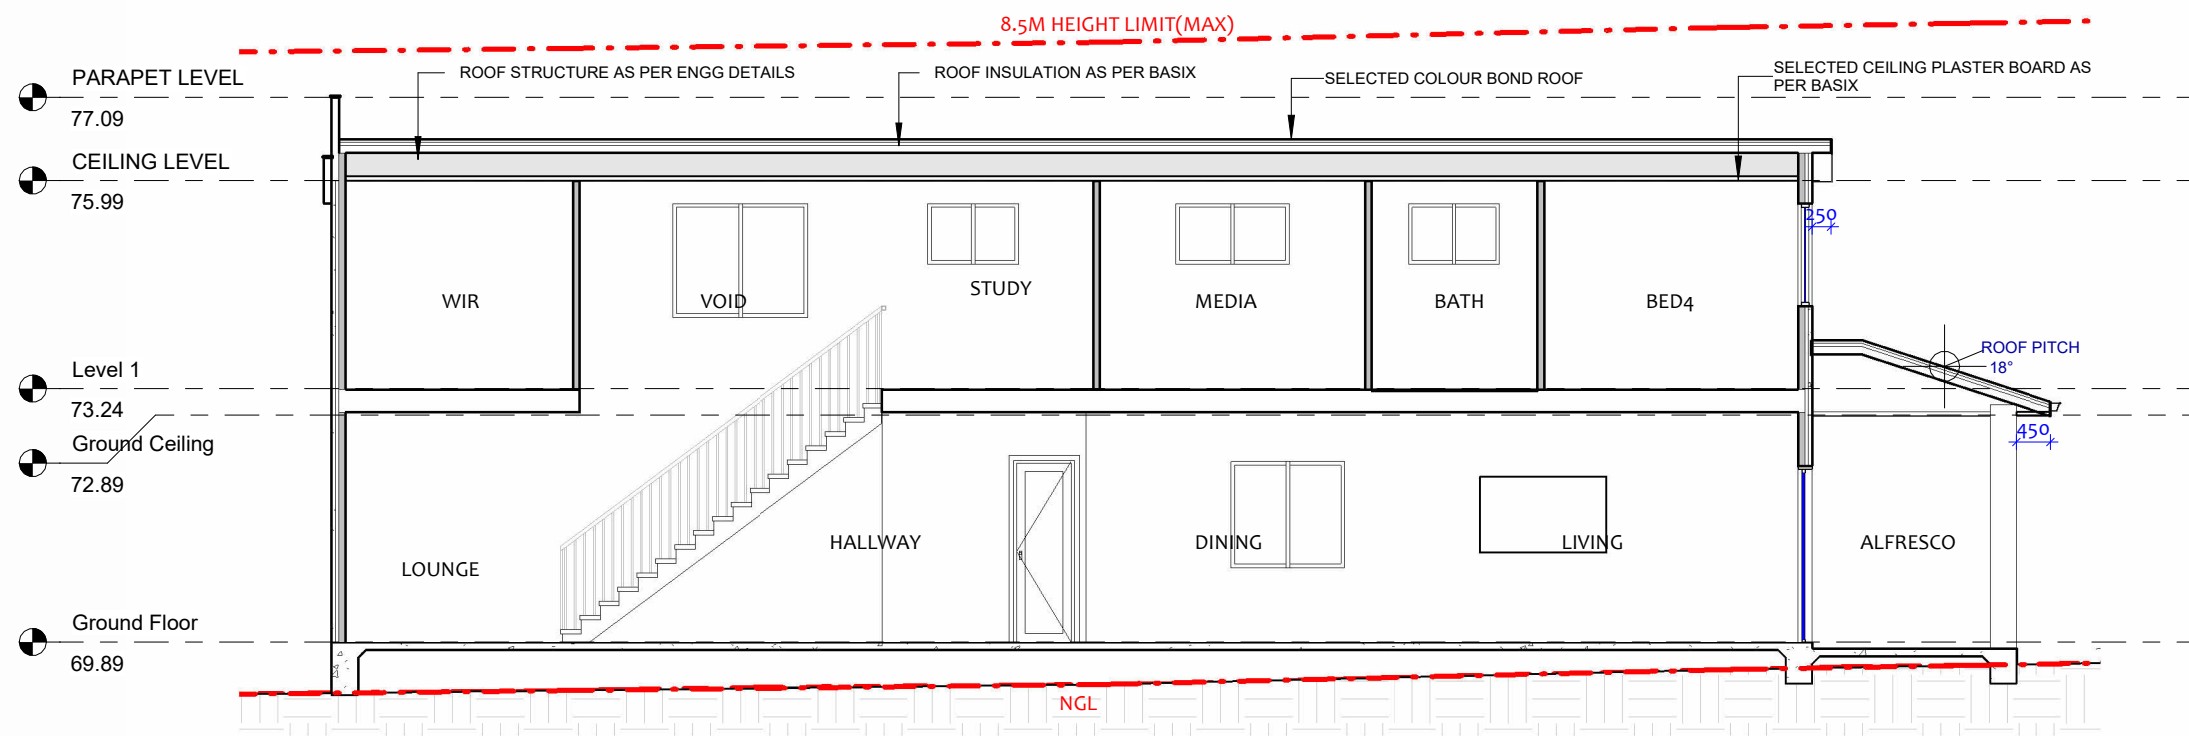

2 LONGITUDINAL SECTION
1 : 100

REV	DATE	DESCRIPTION	BY
6	20-08-2025	CDC ISSUE	

RUBY

HOMES

THIS DRAWING IS THE EXCLUSIVE PROPERTY OF THE DEVELOPER & THE REPRODUCTION OF ANY PART WITHOUT THE PRIOR WRITTEN CONSENT OF THE DEVELOPER IS A VIOLATION OF APPLICABLE LAWS. IN NO EVENT SHALL THE DEVELOPER BE HELD LIABLE FOR SPECIAL COLLATERAL, INCIDENTAL OR CONSEQUENTIAL LIABILITY IN CONNECTION WITH THE USE OF THIS DIGITAL DATA ONCE RELEASED FROM THE DEVELOPER'S OFFICE. THIS DRAWING IS TO BE READ & UNDERSTOOD IN CONJUNCTION WITH THE STRUCTURAL, MECHANICAL, ELECTRICAL & / OR ANY OTHER CONSULTANT'S DOCUMENTATION AS MAY BE APPLICABLE TO THE PROJECT PRIOR TO THE START OF ANY WORKS AND FOR ITS DURATION.

PROJECT:

29 DEW STREET
AUSTRAL
LOT 15 29 DEW STREET
AUSTRAL

DRAWING TITLE:

SECTIONS

NORTH:

LOT NO:

15

DRAWN BY:

AS

DRAFTED BY:

SL

DATE:

7-09-2026

CHECKED BY:

RH

CLIENT NAME:

Abigail & Bhikinkosi Thembinkosi Madondo

SCALE:

1 : 100

DRAWING No:

6


REV:

6

ISSUED BY:


CDC ISSUE

CDC.10

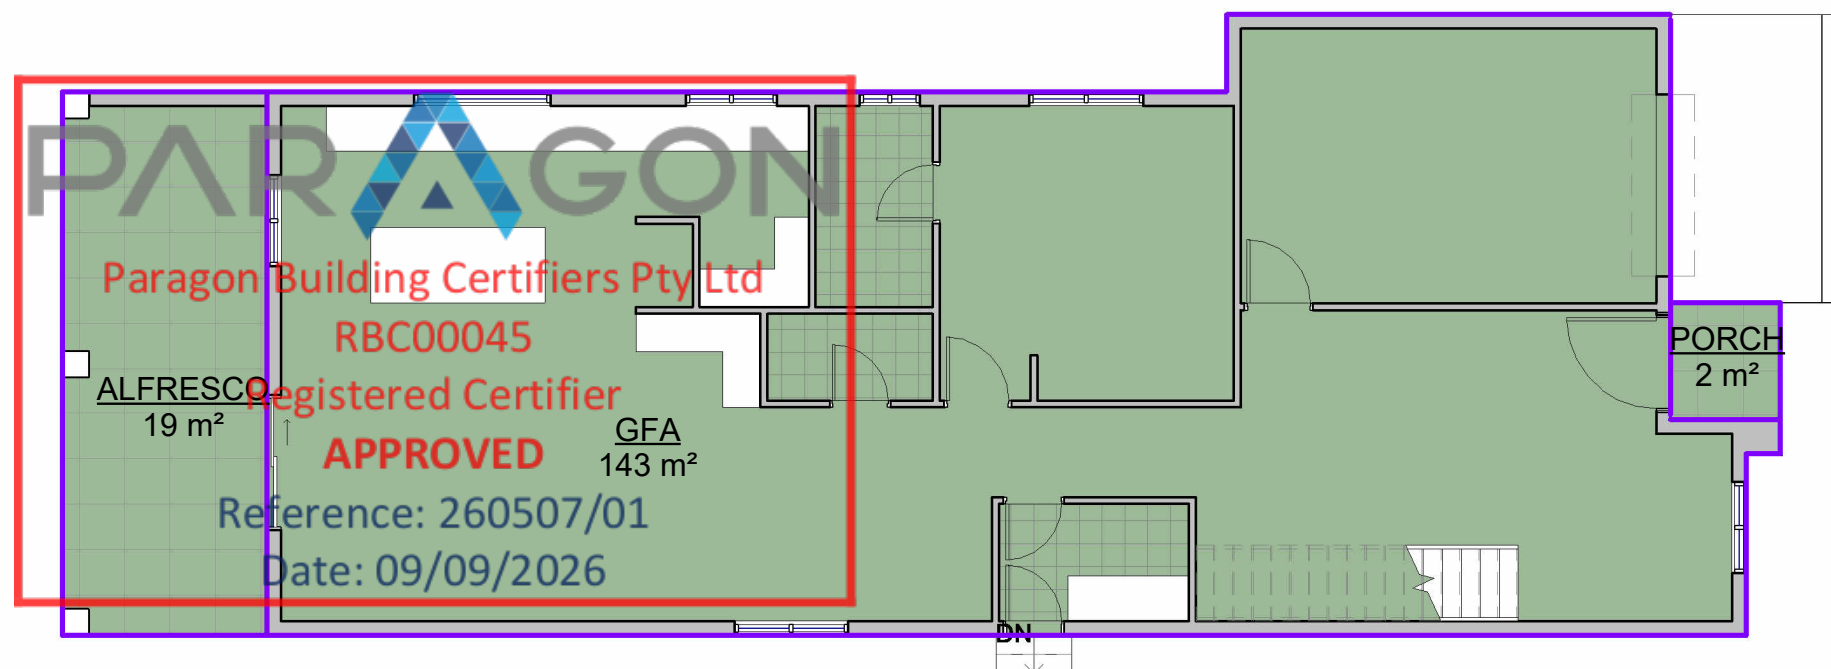

Area Schedule (Gross Building)	
Name	Area
Ground Floor	
ALFRESCO	19 m²
GFA	143 m²
PORCH	2 m²
Ground Floor: 3	164 m²
Level 1	
FFA	125 m²
BALCONY	5 m²
STAIRCASE VOID	11 m²
Level 1: 3	141 m²
Grand total: 6	306 m²

1 Ground Floor
1 : 100

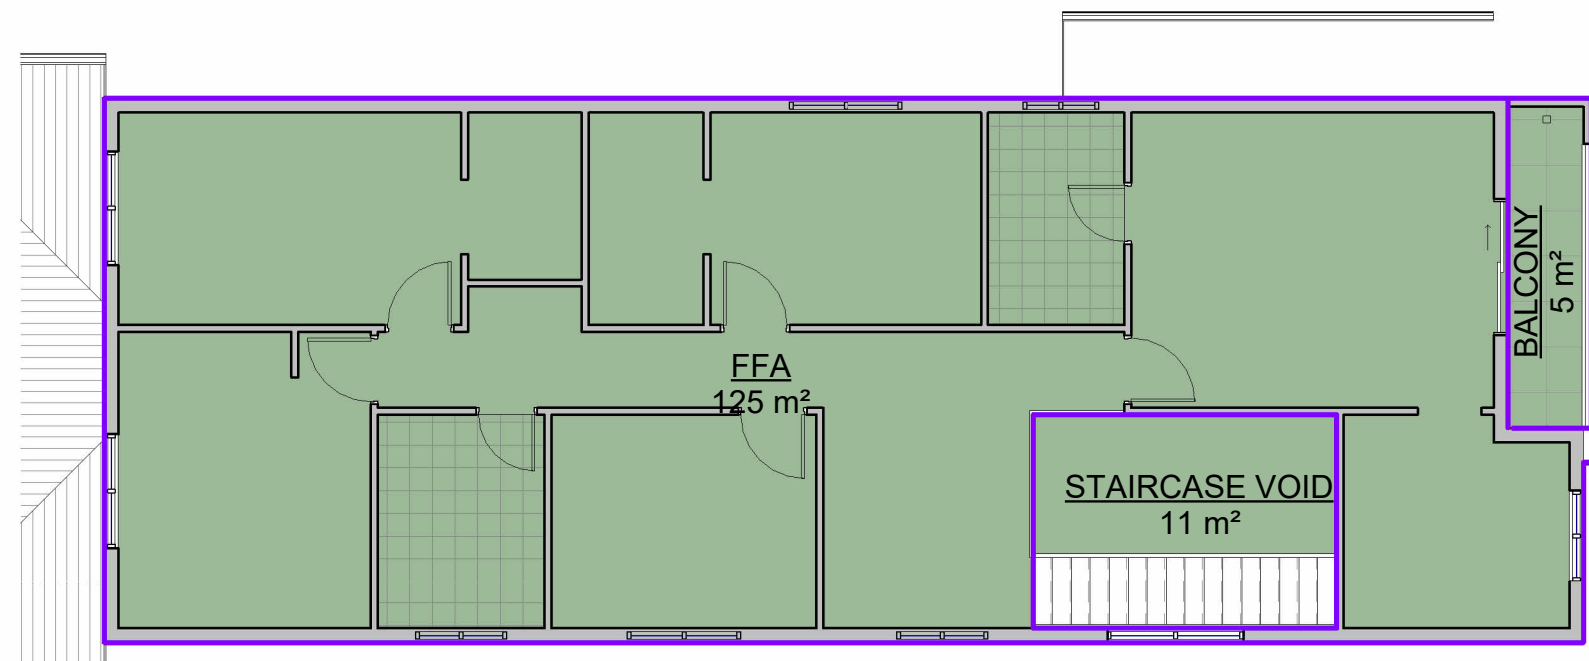

2 Level 1
1 : 100


REV	DATE	DESCRIPTION	BY
6	20-08-2025	CDC ISSUE	
2	24-07-2025	Revision 2	
1	16-07-2025	Concept Issue	



THIS DRAWING IS THE EXCLUSIVE PROPERTY OF THE DEVELOPER & THE REPRODUCTION OF ANY PART WITHOUT THE PRIOR WRITTEN CONSENT OF THE DEVELOPER IS A VIOLATION OF APPLICABLE LAWS. IN NO EVENT SHALL THE DEVELOPER BE HELD LIABLE FOR SPECIAL COLLATERAL, INCIDENTAL OR CONSEQUENTIAL LIABILITY IN CONNECTION WITH THE USE OF THIS DIGITAL DATA ONCE RELEASED FROM THE DEVELOPER'S OFFICE. THIS DRAWING IS TO BE READ & UNDERSTOOD IN CONJUNCTION WITH THE STRUCTURAL, MECHANICAL, ELECTRICAL & / OR ANY OTHER CONSULTANT'S DOCUMENTATION AS MAY BE APPLICABLE TO THE PROJECT PRIOR TO THE START OF ANY WORKS AND FOR ITS DURATION.


PROJECT:
29 DEW STREET AUSTRAL
LOT 15 29 DEW STREET AUSTRAL

DRAWING TITLE:
FLOOR AREA PLAN

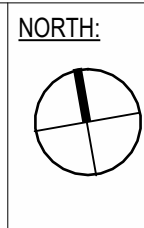


LOT NO:	DATE:	SCALE:	DRAWING No:	REV:
15	7-09-2026	1 : 100	CDC.11	6
DRAWN BY:	CHECKED BY:			ISSUED BY:
AS	RH			
DRAFTED BY:	CLIENT NAME:			
SL	Abigail & Bhekinkosi Thembinkosi Madondo			

CDC ISSUE

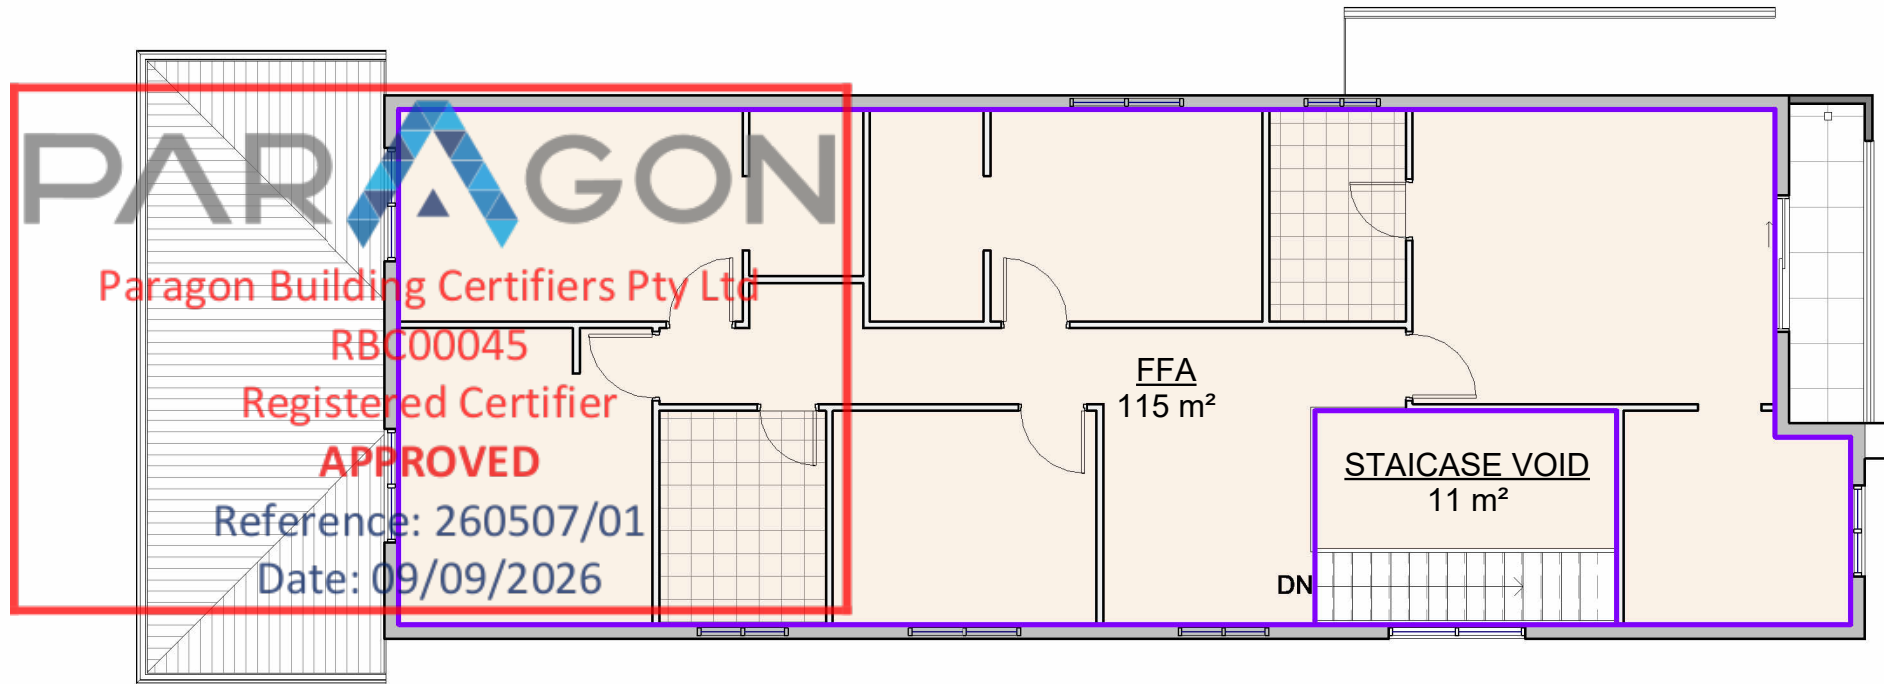

2 Level 1
1 : 100

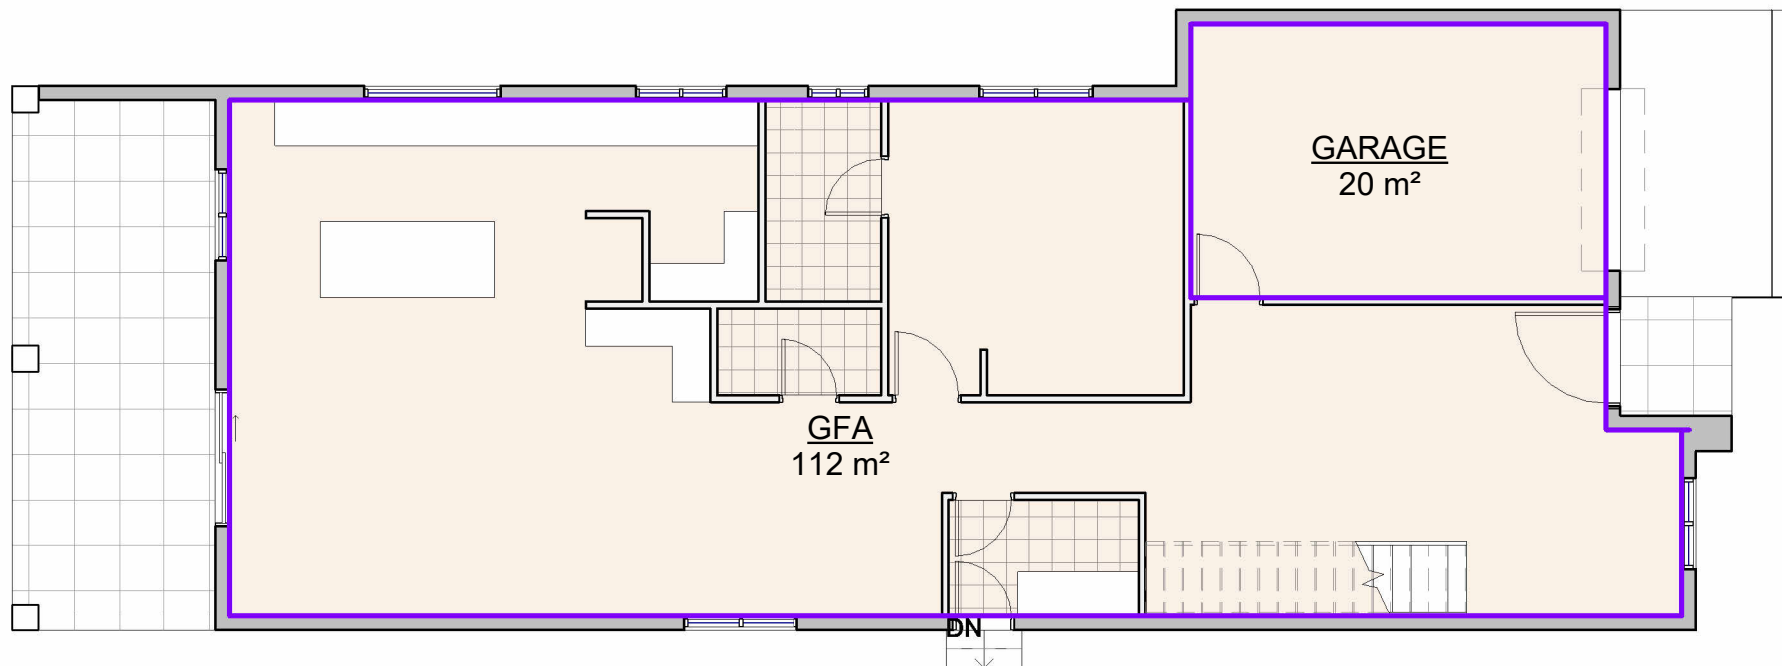

1 Ground Floor
1 : 100

Area Schedule (Rentable)	
Name	Area

Not Placed	
GARAGE	Not Placed
GARAGE	Not Placed
GARAGE	Not Placed
Not Placed: 3	0 m²
Ground Floor	
GFA	112 m²
GARAGE	20 m²
Ground Floor: 2	132 m²
Level 1	
FFA	115 m²
STAIRCASE VOID	11 m²
Level 1: 2	127 m²
Grand total: 7	259 m²


REV	DATE	DESCRIPTION	BY
6	20-08-2025	CDC ISSUE	



THIS DRAWING IS THE EXCLUSIVE PROPERTY OF THE DEVELOPER & THE REPRODUCTION OF ANY PART WITHOUT THE PRIOR WRITTEN CONSENT OF THE DEVELOPER IS A VIOLATION OF APPLICABLE LAWS. IN NO EVENT SHALL THE DEVELOPER BE HELD LIABLE FOR SPECIAL COLLATERAL, INCIDENTAL OR CONSEQUENTIAL LIABILITY IN CONNECTION WITH THE USE OF THIS DIGITAL DATA ONCE RELEASED FROM THE DEVELOPER'S OFFICE. THIS DRAWING IS TO BE READ & UNDERSTOOD IN CONJUNCTION WITH THE STRUCTURAL, MECHANICAL, ELECTRICAL & / OR ANY OTHER CONSULTANT'S DOCUMENTATION AS MAY BE APPLICABLE TO THE PROJECT PRIOR TO THE START OF ANY WORKS AND FOR ITS DURATION.

PROJECT:
29 DEW STREET
AUSTRAL
LOT 15 29 DEW STREET
AUSTRAL

DRAWING TITLE:
RENTABLE AREA
PLAN

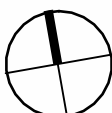NORTH:


LOT NO:
15
DRAWN BY:
AS
DRAFTED BY:
SL

DATE:
7-09-2026
CHECKED BY:
RH

SCALE:
1 : 100

CLIENT NAME:
Abigail & Bhengkosi Thembinkosi Madondo

CDC ISSUE

DRAWING No:
CDC.12
REV:
6
ISSUED BY:



Paragon Building Certifiers Pty Ltd

RBC00045

Registered Certifier

APPROVED

Reference: 260507/01

Date: 09/09/2026



	1. RF	2. HEBEL	3. AL	4. ED	5. GD	6. FAS	7. GUT
	ROOF	HEBEL	WINDOWS/ BALUSTRADE	MAIN DOOR	GARAGE DOOR	FASCIA	GUTTER
MATERIAL	COLORBOND	HEBEL	ALUMINIUM	TIMBER	COLORBOND	COLORBOND	COLORBOND
COLOUR							

NOTE : ALL COLOURS SPECIFIED ARE INDICATIVE ONLY AND ARE SUBJECT TO VARIATION AND TO AVAILABILITY
ANY DISCREPANCY PLEASE FOLLOW AS PER RENDERED IMAGE

CDC ISSUE

6	20-08-2025	CDC ISSUE	
REV	DATE	DESCRIPTION	BY





THIS DRAWING IS THE EXCLUSIVE PROPERTY OF THE DEVELOPER & THE REPRODUCTION OF ANY PART WITHOUT THE PRIOR WRITTEN CONSENT OF THE DEVELOPER IS A VIOLATION OF APPLICABLE LAWS. IN NO EVENT SHALL THE DEVELOPER BE HELD LIABLE FOR SPECIAL COLLATERAL, INCIDENTAL OR CONSEQUENTIAL LIABILITY IN CONNECTION WITH THE USE OF THIS DIGITAL DATA ONCE RELEASED FROM THE DEVELOPER'S OFFICE. THIS DRAWING IS TO BE READ & UNDERSTOOD IN CONJUNCTION WITH THE STRUCTURAL, MECHANICAL, ELECTRICAL & / OR ANY OTHER CONSULTANT'S DOCUMENTATION AS MAY BE APPLICABLE TO THE PROJECT PRIOR TO THE START OF ANY WORKS AND FOR ITS DURATION.

PROJECT:
**29 DEW STREET
AUSTRAL**
LOT 15 29 DEW STREET
AUSTRAL

DRAWING TITLE:
COLOR SCHEDULE

NORTH:

LOT NO: 15	DATE: 7-09-2026	SCALE: 1 : 100	DRAWING No: CDC.14	REV: 6
DRAWN BY: AS	CHECKED BY: RH	ISSUED BY:		
DRAFTED BY: SL	CLIENT NAME: Abigail & Bhekinkosi Thembinkosi Madondo			

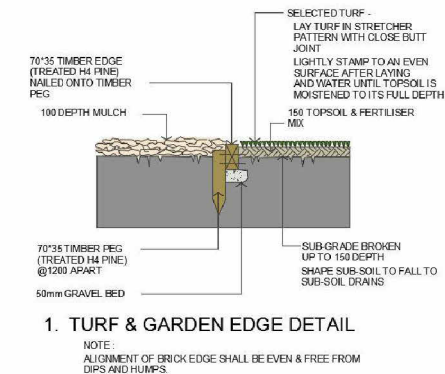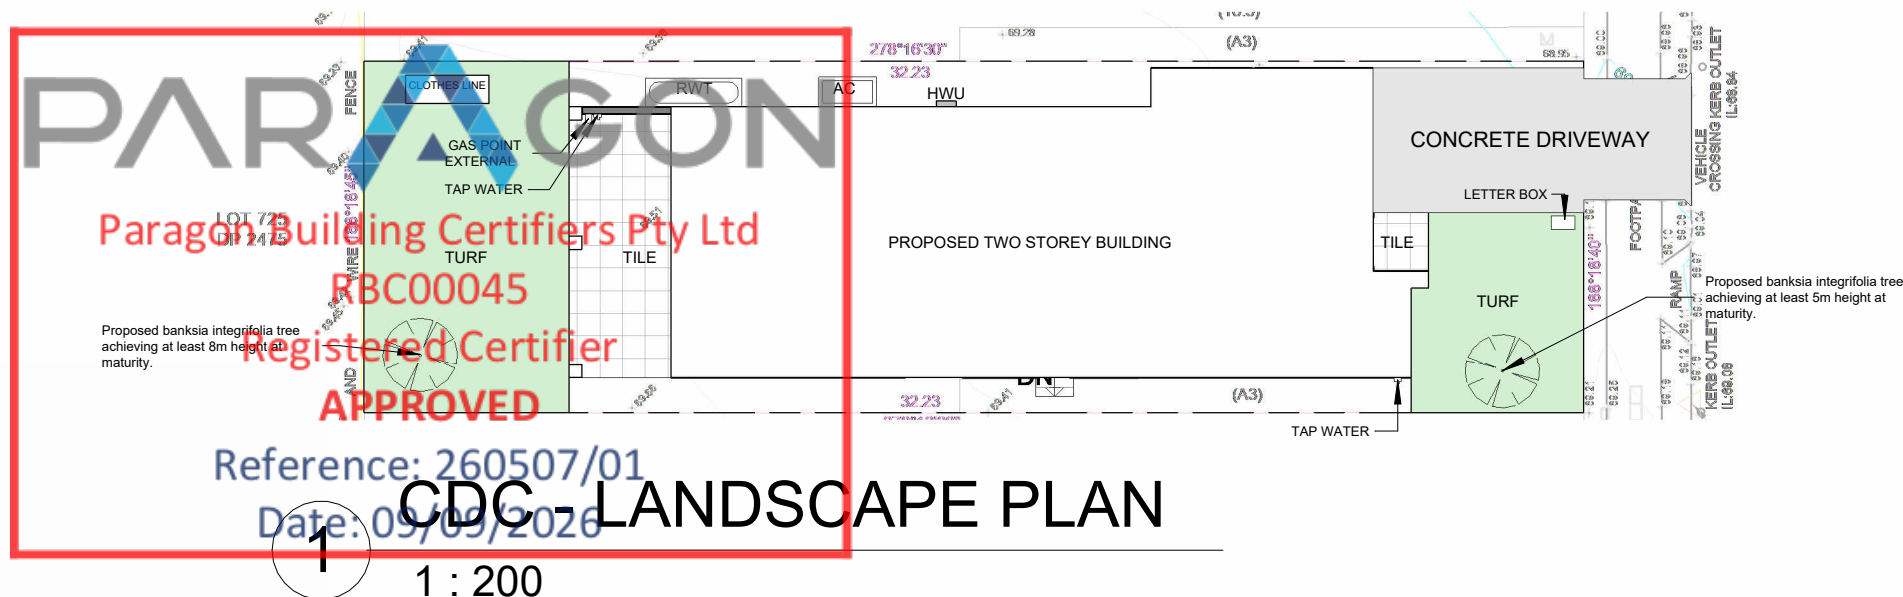

GENERAL NOTES:

- LANDSCAPE CONTRACTOR TO CHECK DA CONDITIONS AND STAMPED LANDSCAPE PLAN BEFORE COMMENCING WORKS TO ENSURE NO ADDITIONS/AMENDMENTS TO PLAN.
- GARDEN BEDS IN OSD BASIN TO CONSIST OF NON FLOATABLE DECORATIVE GRAVEL.
- REFER TO HYDRAULICS ENGINEERS PLAN FOR OSD DETAILS/FINAL LEVELS.
- MULCHED PLANTING BEDS TO BE A MINIMUM DEPTH OF 75mm AS SELECTED.
- CONTRACTOR'S RESPONSIBILITY TO CHECK AND ADJUST SOIL pH AS REQUIRED.
- PROVIDE TIMBER EDGE AS A MINIMUM BENEATH FENCING/GATES TO DEFINE TURF AND GARDEN BEDS/PATHWAYS. EDGING TO BE PROVIDED TO ALL AREAS WHERE DIFFERING MATERIALS MEET i.e TURF/GARDEN, TURF/GRAVEL PATH ETC.
- WEED MAT BENEATH GRAVEL GRAVEL PATHWAYS REQUIRED TO LIMIT MUD TRACKING.
- PREMIUM ORGANIC GARDEN MIX TO BE USED.
- ALL PLANTS TO BE HEALTHY AND VIGOROUS.
- CONTRACTOR TO MAKE GOOD TURF ON NATURE STRIP POST CONSTRUCTION
- CONTRACTOR TO MAKE GOOD TURF ON NATURE STRIP POST CONSTRUCTION.
- DO NOT SCALE ARCHITECTURAL SETOUT FROM LANDSCAPE DRAWING.
- EXISTING TREE SPREAD APPROXIMATE ONLY. REFER TO TREE REPORT WHEN APPLICABLE.
- SITE SURVEY PROVIDED BY OTHERS.
- BUFFALO TURF PREFERRED OVER KIKUYU.


LANDSCAPE BASIX NOTE:
THE APPLICANT MUST PLANT INDIGENEOUS OR LOW WATER USE SPECIES OF VEGETATION THROUGHOUT 15 SQM OF THE SITE.

NOTE : BUILDER RESERVES THE RIGHT NOT TO UNDERTAKE NOR SUPPLY CERTIFICATE FOR OCCUPATION CERTIFICATE.
NOTE : TO AID COMPLIANCE WITH BASIX LEGISLATION, PLANTS (WHERE APPLICABLE) HAVE BEEN SELECTED FROM THE LOCAL CITY COUNCIL/SHIRE PLANT LISTS.
NOTE: LOCATION OF SEWER MAINS/LINES, WATER PIPES, UNDERGROUND ELECTRICITY AND OTHER SERVICES MUST BE OBTAINED PRIOR TO COMMENCEMENT OF ANY WORK ON SITE.

CONTRACTORS NOTE : CALCULATED AREAS DETERMINED BY CAD AND HAVE BEEN ROUNDED UP FOR USE AS A GUIDE ONLY. ALLOW STANDARD PERCENTAGE FOR CUTTING AND WASTAGE. CONFIRM DIMENSIONS AND NUMBERS PRIOR TO QUOTING/ORDERING.

LANDSCAPE AREA

FRONT AREA	23.3 m ²
BACKYARD AREA	50.33 m ²
TOTAL AREA	73.63 m ²

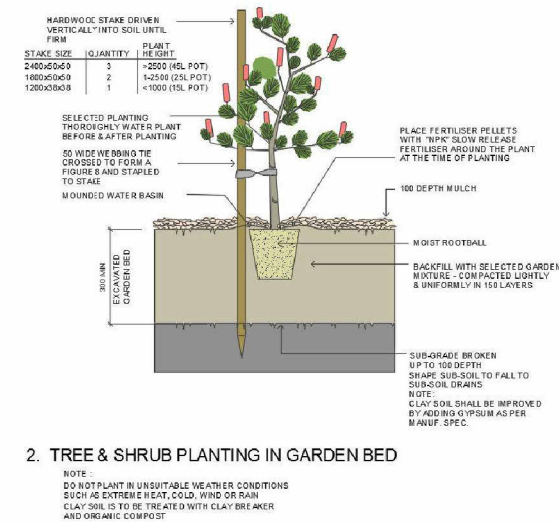


REV	DATE	DESCRIPTION	BY
6	20-08-2025	CDC ISSUE	

RUBY HOMES

THIS DRAWING IS THE EXCLUSIVE PROPERTY OF THE DEVELOPER & THE REPRODUCTION OF ANY PART WITHOUT THE PRIOR WRITTEN CONSENT OF THE DEVELOPER IS A VIOLATION OF APPLICABLE LAWS. IN NO EVENT SHALL THE DEVELOPER BE HELD LIABLE FOR SPECIAL COLLATERAL, INCIDENTAL OR CONSEQUENTIAL LIABILITY IN CONNECTION WITH THE USE OF THIS DIGITAL DATA ONCE RELEASED FROM THE DEVELOPER'S OFFICE. THIS DRAWING IS TO BE READ & UNDERSTOOD IN CONJUNCTION WITH THE STRUCTURAL, MECHANICAL, ELECTRICAL & / OR ANY OTHER CONSULTANT'S DOCUMENTATION AS MAY BE APPLICABLE TO THE PROJECT PRIOR TO THE START OF ANY WORKS AND FOR ITS DURATION.

PROJECT:
29 DEW STREET AUSTRAL
LOT 15 29 DEW STREET AUSTRAL

DRAWING TITLE:
LANDSCAPE PLAN

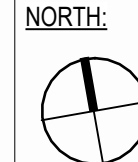

LOT NO:	DATE:	SCALE:	DRAWING No:	REV:
15	7-09-2026	1 : 200	CDC.15	6
DRAWN BY:	CHECKED BY:	ISSUED BY:		
AS	RH			
DRAFTED BY:	CLIENT NAME:			
SL	Abigail & Bhengkosi Thembinkosi Madondo			


CDC ISSUE

10.2.1 Wet Areas


1. Building elements in wet areas within a building must be protected with a waterproofing system.
2. The waterproofing system in (1) must be either waterproof or water resistant in accordance with 10.2.2 to 10.2.6.

1. For a shower area with a hob, step-down or level threshold, the following applies:
 - a. The floor of the shower area must be **waterproof** including any hob or step-down (see Figure 10.2.2) and
 - b. The walls of the shower area must be **waterproof** not less than 1800 mm above the floor substrate (see Figure 10.2.2).
 - c. Wall junctions and joints within the shower area must be **waterproof** not less than 40 mm either side of the junction (see Figure 10.2.2).
 - d. Wall/floor junctions within the shower area must be **waterproof** (see Figure 10.2.2).
 - e. Penetrations within the shower area must be **waterproof**.
2. A shower with a **preformed shower base** must also comply with the requirements of (1), except for (a) which is not applicable.

Figure 10.2.2: Extent of treatment for shower areas - concrete compressed fibre-cement and fibre-cement sheet floors.

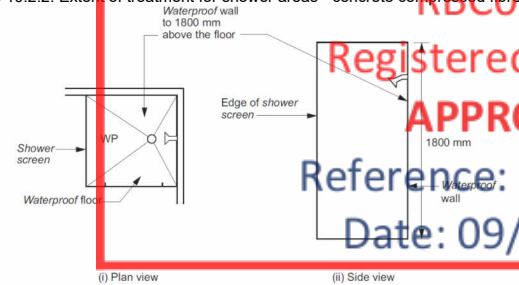

(a) Enclosed shower

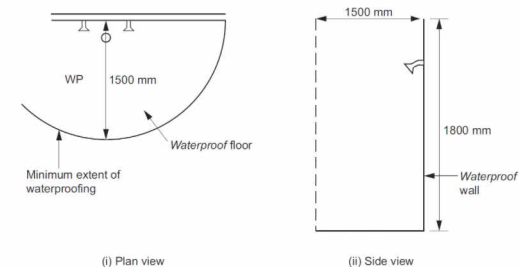

(b) Unenclosed shower

Figure Notes

Wall/floor junction heights are to be as per 10.2.2 to 10.2.6 (as applicable).

Notes

Where a shower is above a bath or spa, use requirements for shower.

10.2.3 Area outside shower area

1. For concrete, compressed fibre-cement and fibre-cement sheet flooring, the floor of the room must be water resistant.
2. For timber floors including particleboard, plywood and other timber based flooring materials, the floor of the room must be waterproof.
3. Wall/floor junctions must be -
 - a. waterproof, and
 - b. where a flashing is used, the horizontal leg must be not less than 40 mm.

10.2.4 Areas adjacent to baths and spas without showers

- | | | |
|----|---|---------------------------------------|
| 1. | For areas adjacent to all baths and spas, the following applies: | |
| a. | For concrete, compressed fibre-cement and fibre-cement sheet flooring, the floor of the room must be water resistant. | |
| b. | For timber floors including particleboard, plywood and other timber based flooring materials, the floor of the room must be waterproof. | |
| c. | Tap and spout penetrations must be waterproof where they occur in horizontal surfaces. | |
| 2. | For areas adjacent to non-freestanding baths and spas, the following applies: | |
| a. | Walls must be water resistant (see Figure 10.2.4a and Figure 10.2.4b)- | |
| | • to a height of not less than 150mm above the vessel, for the extent of the vessel, where the vessel is within 75mm of a wall junction | |
| | • for all exposed surfaces below vessel lip. | |
| b. | Wall junctions and joints must be water resistant within 150mm above a vessel for the extent of the vessel. | |
| c. | Wall/floor junctions must be waterproof for the extent of the vessel (see Figure 10.2.4a and Figure 10.2.4b). | Waterproof wall junction |
| 3. | For inserted baths and spas, the following applies. | |
| a. | For floors and horizontal surfaces: | |
| | • Any shelf area adjoining the bath or spa must be waterproof and include a waterstop under the vessel lip. | |
| | • There are no requirements for the floor under a bath or spa. | Waterproof floor under bath or spa |
| b. | For walls: | |
| | • Waterproof to not less than 150mm above the lip of a bath or spa. | |
| | • There are no requirements for the floor under a bath or spa. | |
| c. | For wall junctions and joints, the following applies: | |
| | • Waterproof junctions within 150mm of a bath or spa. | |
| | • There are no requirements for junctions and joints in walls beneath the lip of a bath or spa. | |
| d. | Tap and spout penetrations must be waterproof where they occur in horizontal surfaces. | Waterproof tap and spout penetrations |

Figure 10.2.4a: Areas adjacent to baths and spas without showers for concrete, compressed fibre-cement and fibre-cement sheet flooring


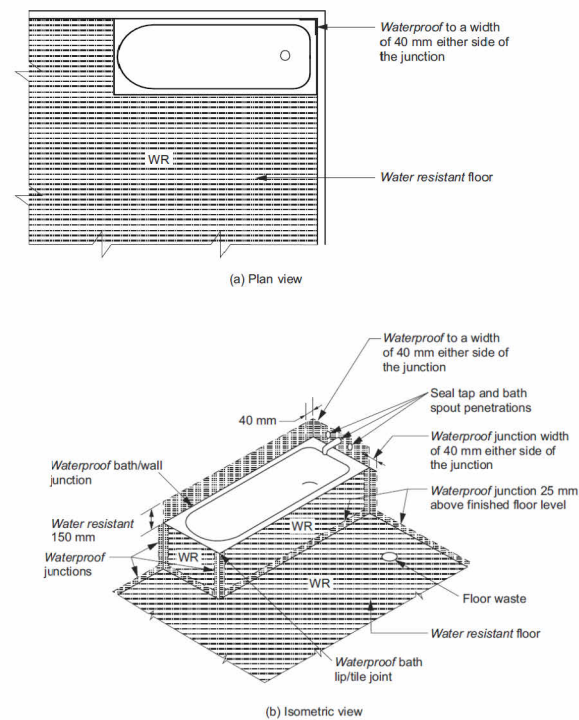



Figure 10.2.4b: Areas adjacent to baths and spas without showers for timber floors including particle-board, plywood and other floor materials

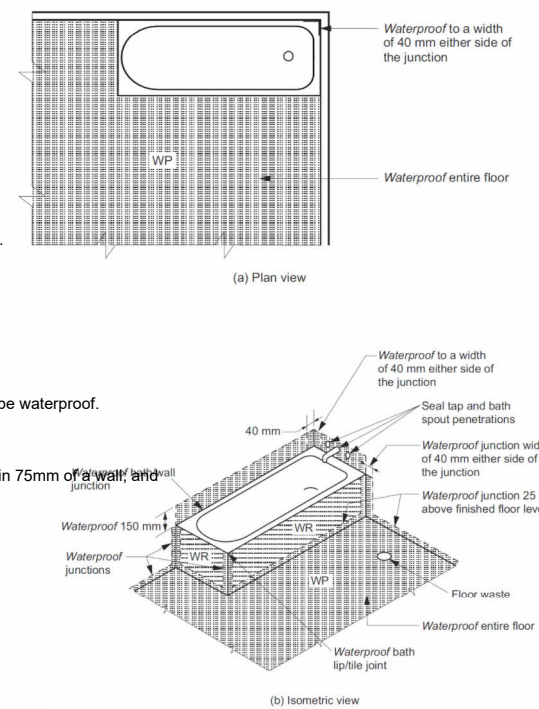

- ### 10.2.5 Other areas

1. For walls adjoining other types of vessels (e.g. sink, basin or laundry tub), the following applies:
 - a. Walls must be water resistant to a height of not less than 150mm above the vessel, for the extent of the vessel, where the vessel is withing 75 mm of a wall (see Figure 10.2.5.)
 - b. Waterproof wall junctions where a vessel is fixed to a wall.
 - c. Waterproof tap and spout penetrations where they occur in surfaces required to be waterproof or water resistant.
2. For laundries and WCs, the following applies:
 - a. The floor of the room must be water resistant.
 - b. Wall/floor junctions must be water resistant, and where a flashing is used, the horizontal leg must not be less than 40 mm.
3. For WCs with handheld bidet spray installations, the following applies:
 - a. The floor of the room must be waterproof.
 - b. Walls must be -
 - waterproof in WC area within a 900 mm radius from the wall connection of the handheld bidet spray device to a height of not less than 150mm above the floor substrate; and
 - water resistant in WC area within a 900 mm radius from the wall connection of the handheld bidet device to not less than 1200 mm above the finished floor level of the WC.
 - c. Wall junctions within the WC area within 900 mm radius from the wall connection of the handheld bidet spray device must be waterproof.
 - d. Wall/floor junctions within the WC area within 1000 mm radius from the wall connection of the handheld bidet spray device must be waterproof.
 - e. Penetrations in the WC area must be waterproof.

Figure 10.2.5: Bath and vessel abutting wall - areas to be protected

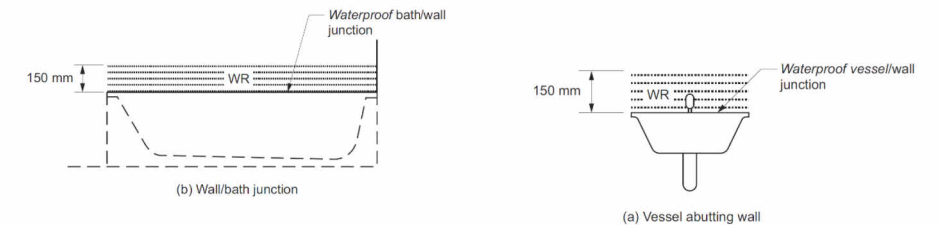

10.2.6 Waterproofing systems

1. For the purposes of this Part, a waterproofing system is deemed -
 - a. waterproof, if it complies with (2); or
 - b. water resistant, if it complies with (3).
2. For a waterproofing system required to be waterproof in accordance with 10.2.2 to 10.2.5, the materials nominated in 10.2.8 must be used.
3. For a waterproofing system required to be water resistant in accordance with 10.2.2 to 10.2.5, the materials nominated in 10.2.9 must be used in conjunction with the materials in 10.2.10.

10.2.12 Construction of wet area floors - falls

Where a floor waste is installed -

- the minimum continuous fall of a floor plane to the waste must be 1:80; and
- the maximum continuous fall of a floor plane to the waste must be 1:50.

				CDC ISSUE								
				 THIS DRAWING IS THE EXCLUSIVE PROPERTY OF THE DEVELOPER & THE REPRODUCTION OF ANY PART WITHOUT THE PRIOR WRITTEN CONSENT OF THE DEVELOPER IS A VIOLATION OF APPLICABLE LAWS. IN NO EVENT SHALL THE DEVELOPER BE HELD LIABLE FOR SPECIAL COLLATERAL, INCIDENTAL OR CONSEQUENTIAL LIABILITY IN CONNECTION WITH THE USE OF THIS DIGITAL DATA ONCE RELEASED FROM THE DEVELOPER'S OFFICE. THIS DRAWING IS TO BE READ & UNDERSTOOD IN CONJUNCTION WITH THE STRUCTURAL, MECHANICAL, ELECTRICAL & / OR ANY OTHER CONSULTANT'S DOCUMENTATION AS MAY BE APPLICABLE TO THE PROJECT PRIOR TO THE START OF ANY WORKS AND FOR ITS DURATION.	PROJECT: 29 DEW STREET AUSTRAL LOT 15 29 DEW STREET AUSTRAL	DRAWING TITLE: WATERPROOFING DETAILS	NORTH:	LOT NO:	DATE:	SCALE: 1 : 50	DRAWING No:	REV:
15	7-09-2026	CDC.16	6									
DRAWN BY:	CHECKED BY:							ISSUED BY:				
AS	RH											
DRAFTED BY:	CLIENT NAME:											
SL	Abigail & Bhekinkosi Thembinkosi Madondo											
REV	DATE	DESCRIPTION		BY								