PROPOSED DOUBLE STOREY RESIDENCE

7 CATALANA STREET SPRING FARM 2570 LOT 43, DP1316318

Copyright HIRA DESIGNS ©

Notes
1. CONTRACTOR MUST VERIFY ALL DIMENSIONS ON SITE BEFORE COMMENCING WORK OR PREPARING SHOP DRAWINGS.
2. DO NOT SCALE DRAWINGS.
3. CONTRACTOR TO CHECK UNDERGROUND SERVICES BEFORE COMMENCING WORKS BY CONTACTING DIAL BEFORE YOU DIG. IF DIAL BEFORE YOU DIG INFORMATION IS PROVIDED WITH THIS DOCUMENTATION IT SHALL BE ASSUMED NOT TO BE CURRENT AND CONTRACTOR SHALL MAKE THEIR OWN ENQUIRES.



3D VIEW DIGRAMATIC ONLY

PLEASE NOTE THAT WINDOWS & DOORS MAY VARY DEPENDING ON BUILDER'S SELECTED WINDOW & DOOR SUPPLIER . LANDSCAPING & INTERNAL FURNITURE TO BE DONE BY OWNER AND IS SHOWN FOR VISULATION PURPOSES ONLY .FURTHERMORE MATERIAL FINISH MAY VARY AS PER FINISHES SCHEDULE

Drawing No:	Description	Issue / Rev
CDC-000	COVER	-
CDC-001	GENERAL SPECIFICATIONS	-
CDC-002	BUILDING SPECIFICATION 1	-
CDC-003	BUILDING SPECIFICATION 2	-
CDC-004	BUILDING SPECIFICATION 3	-
CDC-100	SITE PLAN	-
CDC-101	SLAB PLAN	-
CDC-102	CUT & FILL	
CDC-103	GROUND FLOOR PLAN	-
CDC-104	FIRST FLOOR PLAN	-
CDC-105	ROOF PLAN	-
CDC-106	WEST/SOUTH ELEVATIONS	-
CDC-107	EAST/NORTH ELEVATIONS	-
CDC-108	SECTION	-
CDC-109	GFA DIAGRAMS	-
CDC-110	SEDIMENT & CONTROL PLAN	-
CDC-111	WINDOW SCHEDULE	-
CDC-112	DOOR SCHEDULE	-
CDC-113	BASIX COMMITMENTS SHEET	-
CDC-114	LANDSCAPE PLAN	-
CDC-115	LANDSCAPE NOTES	-
CDC-116	FINISHES SCHEDULE	-

HIRA DESIGNS ©
This drawing remains the property of Hira Designs. It may be used for the purpose for which it was commissioned & in accordance with the terms of engagement for that commission.

Rev	Description	Date	App'd
-	CDC DRAWING ISSUED FOR APPROVAL	06.08.26	

Project
PROPOSED DOUBLE STOREY RESIDENCE

7 CATALANA STREET, SPRING FARM 2570
LOT 43, DP1316318

HIRA DESIGNS
Business Address: 13 Feathertop Ave, MINTO NSW 2566
Postal Address: 13 Feathertop Ave, MINTO NSW 2566
Phone Number: 0415112594
Email: info@hiradesigns.com.au
Project Designer:
Pramila Maharjan

Drawing Title
CDC DRAWINGS
COVER

Checked/Approved
PM

Scale
@A3 Sheet Size

Project Number
475041

Drawing Number Revision
CDC-000 -

Status
CDC DRAWINGS

STONEGROVE HOMES

BUILDING DESIGN SAFETY NOTES
THESE NOTES MUST BE READ AND UNDERSTOOD BY ALL INVOLVED IN THIS PROJECT.
THIS INCLUDES (BUT IS NOT LIMITED TO): OWNER, BUILDER, SUB-CONTRACTORS, CONSULTANTS, OPERATORS, MAINTAINORS, RENOVATORS, DEMOLISHERS ETC

Copyright HIRA DESIGNS ©

Notes
1. CONTRACTOR MUST VERIFY ALL DIMENSIONS ON SITE BEFORE COMMENCING WORK OR PREPARING SHOP DRAWINGS.
2. DO NOT SCALE DRAWINGS.
3. CONTRACTOR TO CHECK UNDERGROUND SERVICES BEFORE COMMENCING WORKS BY CONTACTING DIAL BEFORE YOU DIG. IF DIAL BEFORE YOU DIG INFORMATION IS PROVIDED WITH THIS DOCUMENTATION IT SHALL BE ASSUMED NOT TO BE CURRENT AND CONTRACTOR SHALL MAKE THEIR OWN ENQUIRES.

1. FALLS, SLIPS & TRIPS

A) WORKING AT HEIGHTS
• During Construction
Wherever possible, components for this building should be prefabricated off-site or at ground level to minimise the risk of workers falling more than 2 m. However, construction of this building will require workers to be working at heights where a fall in excess of two meters is possible and injury is likely to result from such a fall. The builder should provide a suitable barrier wherever a person is required to work in a situation where falling more than two meters is a possibility.

• During operation or maintenance
For houses or other low-rise buildings where scaffolding is appropriate: Cleaning and maintainence of windows, walls, roof or other components of this building will require persons to be situated where a fall from a height in excess of two meters is possible . Where this type of activity is required, scaffolding, ladders or trestles should be used in accordance with relevant codes of practice, regulations or legislation.

B) SLIPPERY OR UNEVEN SURFACES All the floor finishes have been selected by the Builder/Owner. The Architect has not been involved in the selection of surface finishes. The owner is responsible for the selection of surface finishes in the pedestrian trafficable areas of this building. Surfaces should be selected in accordance with AS HB 197:1999 and AS/NZ 4586:2004.

C) STEPS, LOOSE OBJECTS AND UNEVEN SURFACES Due to design restrictions for this building, steps and/or ramps are included in the building which may be a hazard to the workers carrying objects or otherwise occupied. Steps should be clearly marked with both visual and tactile warning during construction, maintenance, demolition and at all times when the building operates as a workplace. Building owners and occupiers should monitor the pedestrian access ways and in particular access to areas where maintenance is routinely carried out to ensure that surfaces have not moved or cracked so that they become uneven and present a trip hazard. Spills, loose material, stray objects or any other matter that may cause a slip or trip hazard. Spills, loose material, stray objects or any other matter that may cause a slip or trip hazard should be cleaned or removed from access ways. Contractors should be required to maintain a tidy work site during construction, maintenance or demolition to reduce the risk of trips and falls in the workplace. Materials for construction or maintenance should be stored in designated areas away from access ways and work areas.

2. TRAFFIC MANAGEMENT
A) FOR BUILDING ON A MAJOR ROAD, NARROW ROAD OR STEEPLY SLOPING ROAD: Parking of vehicles or loading/unloading of vehicles on this roadway may cause a traffic hazard. During construction, maintenance or demolition of this building designated parking for workers and loading areas should be provided. Trained traffic management personnel should be responsible for the supervision of these areas.

B) FOR BUILDING WHERE ON-SITE LOADING/UNLOADING IS RESTRICTED: Construction of this building will require loading and unloading of materials on the roadway. Deliveries should be well planned to avoid congestion of the loading areas and trained traffic management personnel should be adopted for the work site.

3. FALLING OBJECTS
A) LOOSE MATERIALS OR SMALL OBJECTS
Construction, maintenance or demolition work on or around this building is likely to involve persons working above ground level or above floor levels. Where this occurs one or more of the following measures should be taken to avoid objects falling from the area where the work is being carried out onto persons below:
1. Prevent or restrict access to areas below where the work is being carried out.
2. Provide toeboards to scaffolding or work platforms.
3. Provide protective structure below the work area.
4. Ensure that all persons below the work area have Personal Protective Equipment (PPE).

During Construction, renovation or demolition of this building, parts of the structure including fabricated steelwork, heavy panels and many other components will remain standing prior to or after supporting parts are in place. Contractors should insure that temporary bracing or other required support is in place at all times when collapse which may injure persons in the area is a possibility.

B) BUILDING COMPONENTS: Mechanical lifting of materials and components during construction, maintenance or demolition presents a risk of falling objects. Contractors should ensure that appropriate lifting devices are used, that loads are properly secured and that access to areas below the load is prevented or restricted.

4. MANUAL TASKS
Components within this design with a mass excess of 25kg should be lifted by two or more workers or by mechanical lifting device. Where this is not practical, suppliers or fabricators should be required to limit the component mass. All material packaging, building and maintenance components should clearly show the total mass of packages and where practical all items should be stored on site in a way which minimises bending before lifting. Advice should be provided on safe lifting methods in all areas where lifting may occur.

Construction, maintenance and demolition of this building will require the use of portable tools and equipment. These should be fully maintained in accordance with manufacturer's specifications and not used where faulty or (in the case of electrical equipment) not carrying a current electrical safety tag. All safety guards or devices should be regularly checked and Personal Protective Equipment should be used in accordance with manufacturer's specifications.

5. SERVICES
Rupture of services during excavation or other activity creates a variety of risks including release of hazardous materials. Existing services are located on and around this site. Where known, these are identified on the plans but the exact location and extent of services may vary from that indicated. Services should be located using an appropriate service (such as Dial Before You Dig), appropriate excavation practice should be used and, where necessary, specialist contractors should be used.

A) LOCATIONS WITH UNDERGROUND POWER:
Underground power lines may be located in or around this site. All underground power lines must be disconnected or carefully located and adequate warning signs used prior to any construction, maintenance or demolition commencing.

B) LOCATIONS WITH OVERHEAD POWER LINES:
Overhead power lines may be near or on this site. These pose a risk of electrocution if struck or approached by lifting devices or other plant and persons working above ground level. Where there is a danger of this occurring, power lines should be, where practical, disconnected or relocated. Where this is not practical adequate warning in the form of bright colored tape or signage should be used or a protective barrier provided.

6. HAZARDOUS SUBSTANCES
A) ASBESTOS
For alterations to a building constructed prior to 1990:
1990 - it therefore may contain asbestos
1983 - it therefore is likely to contain asbestos
Asbestos can be in cladding material or in fire retardant insulation material. In either case, the Builder should check and, if necessary, take appropriate action before demolishing, cutting, sanding, drilling or otherwise disturbing the existing structure

B) POWDERED MATERIALS
Many materials used in the construction of this building can cause harm if inhaled in powdered form. Persons working on or in the building during construction, operational maintenance or demolition should ensure good ventilation and wear PPE including protection against inhalation while using powdered material or when sanding, drilling, cutting or otherwise disturbing or creating powdered material.

C) TREATED TIMBER
The design of this building may include provision for the inclusion of treated timber within the structure. Dust or fumes from this material can be harmful. Persons working on or in the building during construction, maintenance or demolition should ensure good ventilation and wear PPE including protection against inhalation of harmful materials when sanding, drilling, cutting or using treated timber in any way that may cause harmful material to be released. Do not burn treated timber.

D) VOLATILE ORGANIC COMPOUNDS
Many types of glue, solvents, spray packs, paints, varnishes and some cleaning materials and disinfectants have dangerous emissions. Areas where these are used should be kept well ventilated while the material is being used and for a period after installation. PPE may also be required. The manufacturer's recommendations for use must be carefully considered at all times.

E) SYNTHETIC MINERAL FIBRE
Fibreglass, rockwool, ceramic and other material used for thermal or sound insulation may contain synthetic mineral fibre which may be harmful if inhaled or if it comes in contact with skin, eyes or other sensitive parts of the body. PPE including protection against inhalation of harmful materials should be used when installing, removing or working near bulk insulation material.

F) TIMBER FLOORS
This building may contain timber floors which have an applied finish. Areas where finishes are applied should be kept well ventilated during construction and for a period after installation. PPE may also be required. The manufacturer's recommendations for use must be carefully considered at all times.

Sydney Wide Certifiers Pty Ltd
Complying Development Certificate
Reference: SWC262403/01
Date: 13/10/2026
Sandres Markhani BDC05035

7. PUBLIC ACCESS

Public access to construction and demolition sites and to areas under maintenance causes risk to workers and public. Warning signs and secure barriers to unauthorised access should be provided. Where electrical installations, excavations, plant or loose materials are present they should be secured when not fully supervised.

8. HIGH RISK ACTIVITY

All electrical work should be carried out in accordance with the code of Practice: Managing Electrical risks at the Workplace, AS/NZ 3012 and all licensing requirements. All work using plant should be carried out in accordance with Code of Practice: Managing risks of plant at the workplace. All work should be carried out in accordance with Code of Practice: Managing Noise and Preventing Hearing Loss at Work. Due to the history of serious incidents it is recommended that particular care be exercised when undertaking work involving steel construction and concrete placement. All the above applies

9. CONFINED SPACES

A) EXCAVATION
Construction of this building and some maintenance on this building will require excavation and installation of items within excavations. Where practical, installation should be carried out using methods which do not require workers to enter the excavation. Where this is not practical adequate support for the excavated area should be provided to prevenet collapse. Warning signs and barriers to prevent accidental or unauthorised access to all excavations should be provided.

B) ENCLOSED SPACES For buildings with enclosed spaces where maintenance or other access may be required. Enclosed spaces within this building may present a risk to persons entering for construction, maintenance or any other purpose. The design documentation calls for warning signs and barriers to unauthorised access. These should be maintained throughout the life of the building. Where workers are required to enter enclosed spaces, air testing equipment and Personal Protective Equipment should be provided.

C) SMALL SPACES For buildings with small spaces where maintenance or other access may be required: Some small spaces within this building will require access by construction or maintenance workers. The design documentation calls for warning signs and barriers to unauthorised access. These should be maintained throughout the life of the building. Where workers are required to enter small spaces they should scheduled so that access is for short periods. Manual lifting and other manual activity should be restricted in small spaces.

10. OPERATIONAL USE OF BUILDING-RESIDENTIAL BUILDINGS

This building has been designed as a residential building. If it, at a later date, it is used or intended to be used as a workplace, the provisions of the Work Health and Safety Act 2011 or subsequent replacement Act should be applied to the new use.

NOTES:-
The following building elements need to be installed as per manufactureres specifications and requirements.
• Roofing
• Capping
• Gutters
• Fascias
• Eaves
• Flashings
• Downpipes
• Brick veneer
• Aluminium Doors & Windows
• Panel lift doors
• Hot water system-mounted on brick wall with recessed Kit
• Air Conditioner
• Solar panels & inverters
• Rain water tank • Smoke alarms
• Mechanical vents
• Fence

ALL BUILDING WORKS TO COMPLY WITH:
• NCC VOLUME 2 BUILDING CODE OF AUSTRALIA 2022
• HOUSING PROVISIONS STANDARD 2022
• ALL RELEVANT AUSTRALIAN STANDARDS (INCLUDING AMENDMENTS)

ALL DRAWINGS TO BE READ IN CONJUCTION WITH THE STRUCTURAL & STORMWATER DESIGN, DRAWINGS AND DETAILS PREPARED BY THE ENGINEER ALL DRAWINGS TO BE READ IN CONJUCTION WITH THE BASIX & NATHERS CERTIFICATE

HIRA DESIGNS ©
This drawing remains the property of Hira Designs. It may be used for the purpose for which it was commissioned & in accordance with the terms of engagement for that commission.

Rev	Description	Date	App'd
-	CDC DRAWING ISSUED FOR APPROVAL	06.08.26	

Project
PROPOSED DOUBLE STOREY RESIDENCE

7 CATALANA STREET, SPRING FARM 2570
LOT 43, DP1316318

HIRA DESIGNS
Business Address: 13 Feathertop Ave, MINTO NSW 2566
Postal Address: 13 Feathertop Ave, MINTO NSW 2566
Phone Number: 0415112594
Email: info@hiradesigns.com.au
Project Designer:
Pramila Maharjan

Drawing Title
CDC DRAWINGS
GENERAL SPECIFICATIONS

Checked/Approved
PM

Scale
@A3 Sheet Size

Project Number
475041

Drawing Number Revision
CDC-001 -

Status
CDC DRAWINGS

STONEGROVE HOMES

Copyright HIRA DESIGNS ©

Notes
1. CONTRACTOR MUST VERIFY ALL DIMENSIONS ON SITE BEFORE COMMENCING WORK OR PREPARING SHOP DRAWINGS.
2. DO NOT SCALE DRAWINGS.
3. CONTRACTOR TO CHECK UNDERGROUND SERVICES BEFORE COMMENCING WORKS BY CONTACTING DIAL BEFORE YOU DIG. IF DIAL BEFORE YOU DIG INFORMATION IS PROVIDED WITH THIS DOCUMENTATION IT SHALL BE ASSUMED NOT TO BE CURRENT AND CONTRACTOR SHALL MAKE THEIR OWN ENQUIRES.

BUILDING SPECIFICATIONS
National Construction Code - Volume 2, Amendment 1 - Building Code of Australia 2022 & Housing Provisions Standard 2022

SITE PREPARATION
- PART 3.1 OF THE NCC VOLUME 2, AMENDMENT 1 - BUILDING CODE OF AUSTRALIA 2022 & HOUSING PROVISIONS STANDARD 2022.

EARTHWORKS
- TO BE CARRIED OUT IN ACCORDANCE WITH THE REQUIREMENTS OF THE ENVIRONMENTAL PLANNING & ASSESSMENT ACT 1979 AND DEVELOPMENT CONSENT CONDITIONS
- PART 3.2 OF THE NCC VOLUME 2, AMENDMENT 1 - BUILDING CODE OF AUSTRALIA 2022 & HOUSING PROVISIONS STANDARD 2022.
- AS 4678:2002 - EARTH-RETAININGSTRUCTURES

DRAINAGE
- PART 3.3 OF THE NCC VOLUME 2, AMENDMENT 1 - BUILDING CODE OF AUSTRALIA 2022 & HOUSING PROVISIONS STANDARD 2022.
- AS/NZS 3500.1:2021 - PLUMBING & DRAINAGE - WATER SERVICES
- AS/NZS 3500.2:2021 - PLUMBING & DRAINAGE - SANITARY PLUMBING & DRAINAGE
- AS/NZS 3500.3:2021 - PLUMBING & DRAINAGE STORMWATER DRAINAGE
- AS/NZS 3500.4:2021 - PLUMBING & DRAINAGE - HEATED WATER SERVICES

STRUCTURAL WORK
- Part 2.2 OF THE NCC VOLUME 2, AMENDMENT 1 - BUILDING CODE OF AUSTRALIA 2022 & HOUSING PROVISIONS STANDARD 2022.
- AS 4100-2020- STEEL STRUCTURES CODES
- AS/NZS 1170.0-2002 - GENERAL PRINCIPLES
- ASNZS 1170.1-2002 - PARTS 1 PERMANENT, IMPOSED AND OTHER ACTIONS
- AS/NZS 1170.2-2021 - PART 2 WIND ACTIONS
- AS 3700-2018- SAA MASONRY CODE
- AS 1684.3-2021- RESIDENTIAL TIMBER FRAMED CONSTRUCTION

FOOTINGS & SLABS
- PART 4 OF THE NCC VOLUME 2, AMENDMENT 1 - BUILDING CODE OF AUSTRALIA 2022 & HOUSING PROVISIONS STANDARD 2022.
- AS 2159:2009 - PILING - DESIGN & INSTALLATION
- AS 2870:2011 - RESIDENTIAL SLABS & FOOTINGS
- AS 3600:2018 - CONCRETE STRUCTURES

MASONRY
- PART 5 OF THE NCC VOLUME 2, AMENDMENT 1 - BUILDING CODE OF AUSTRALIA 2022 & HOUSING PROVISIONS STANDARD 2022.
- AS 3700:2018 - MASONRY STRUCTURES

FRAMING
- PART 6 OF THE NCC VOLUME 2, AMENDMENT 1 - BUILDING CODE OF AUSTRALIA 2022 & HOUSING PROVISIONS STANDARD 2022.
- AS 1684.2:2021 - RESIDENTIAL TIMBER-FRAMED CONSTRUCTION - NON- CYCLONIC AREAS
- AS 1720.1:2010 - TIMBER STRUCTURES - DESIGN METHODS
- AS 4100:2020 - STEEL STRUCTURES
- AS 3660.1-2014 - TERMITE MANAGEMENT SYSTEM

ROOF & WALL CLADDING
- PART 7 OF THE NCC VOLUME 2, AMENDMENT 1 - BUILDING CODE OF AUSTRALIA 2022 & HOUSING PROVISIONS STANDARD 2022.
- AS 1273:1991 - UNPLASTICIZED PVC (UPVC) DOWNPIPES & FITTINGS FORRAINWATER
- AS 1562.1:2018 - DESIGN & INSTALLATION OF SHEET ROOF & WALL CLADDING - METAL
- AS/NZS 1562.3:2006 - DESIGN & INSTALLATION OF SHEET ROOF & WALL CLADDING - PLASTIC
- AS 2049:2002 - ROOF TILES
- AS 2050:2018 - INSTALLATION OF ROOF TILES
- AS 4285:2019 - ROOFLIGHTS

GLAZING
- PART 8 OF THE NCC VOLUME 2, AMENDMENT 1 - BUILDING CODE OF AUSTRALIA 2022 & HOUSING PROVISIONS STANDARD 2022.
- AS 1288:2021 - GLASS IN BUILDINGS -SELECTION & INSTALLATION
- AS 2047:2014 - WINDOWS & EXTERNAL GLAZED DOORS IN BUILDINGS
- AS/NZS 2208:1996 - SAFETY GLAZING MATERIALS IN BUILDINGS

FIRE SAFETY
- PART 9 OF THE NCC VOLUME 2, AMENDMENT 1 - BUILDING CODE OF AUSTRALIA 2022 & HOUSING PROVISIONS STANDARD 2022.
- AS 3786:2014 - SMOKE ALARMS USING SCATTERED LIGHT, TRANSMITTED LIGHTOR IONIZATION

HEALTH & AMENITY
- PART 10 OF THE NCC VOLUME 2, AMENDMENT 1 - BUILDING CODE OF AUSTRALIA 2022 & HOUSING PROVISIONS STANDARD 2022.
- AS/NZS ISO 717.1:2004 - ACOUSTICS - RATING OF SOUND INSULATION IN BUILDINGS & OF BUILDING ELEMENTS -AIRBORNE SOUND INSULATION
- AS ISO 717.2:2004 - ACOUSTICS - RATING OF SOUND INSULATION IN BUILDINGS & OF BUILDING ELEMENTS - IMPACT SOUND INSULATION
- AS 1668.2:2012 - THE USE OF VENTILATION & AIR CONDITIONING IN BUILDINGS - MECHANICAL VENTILATIONIN BUILDINGS
- AS 1668.4:2012 - THE USE OF VENTILATION & AIR CONDITIONING IN BUILDINGS - NATURAL VENTILATION OFBUILDINGS
- AS/NZS 1680.0:2009 - INTERIOR LIGHTING - SAFE MOVEMENT
- AS 3740:2021 - WATERPROOFING OF DOMESTIC WET AREAS
- AS 3000-2018 - ELECTRICAL INSTALLATION
- BCA Part 10.8.1, AS4200.1 & AS4200.2 - PLIABLE BUILDING MEMBRANE INSTALLED.

WATERPROOFING
- PART 10.2 OF THE NCC VOLUME 2, AMENDMENT 1 - BUILDING CODE OF AUSTRALIA 2022 & HOUSING PROVISIONS STANDARD 2022
- AS 3740-2021- WATERPROOFING TO WET AREA
- AS 4654-2012 - EXTERNAL WET AREAS

SAFE MOVEMENT & ACCESS
- PART 11 OF THE NCC VOLUME 2, AMENDMENT 1 - BUILDING CODE OF AUSTRALIA 2022 & HOUSING PROVISIONS STANDARD 2022.
- AS 1428.1:2009 - DESIGN FOR ACCESS &MOBILITY - GENERAL REQUIREMENTS FOR ACCESS - NEW BUILDING WORK
- AS 1657:2018 - FIXED PLATFORMS, WALKWAYS, STAIRWAYS & LADDERS - DESIGN, CONSTRUCTION & INSTALLATION

HANDRAILS & BALUSTRADE
- PART 11.3.3 OF THE NCC VOLUME 2, AMENDMENT 1 - BUILDING CODE OF AUSTRALIA 2022 & HOUSING PROVISIONS STANDARD 2022.
- PART 11.3.4 OF THE NCC VOLUME 2, AMENDMENT 1 - BUILDING CODE OF AUSTRALIA 2022 & HOUSING PROVISIONS STANDARD 2022.
- PART 11.3.5 OF THE NCC VOLUME 2, AMENDMENT 1 - BUILDING CODE OF AUSTRALIA 2022 & HOUSING PROVISIONS STANDARD 2022.
- AS 1288:2021 - GLASS FOR HOUSING - DESIGN & INSTALLATION

PROTECTION OF OPENABLE WINDOW
- PART 11.3.8 OF THE NCC VOLUME 2, AMENDMENT 1 - BUILDING CODE OF AUSTRALIA 2022 & HOUSING PROVISIONS STANDARD 2022.

ENERGY EFFICIENCY
- PART 13 OF THE NCC VOLUME 2, AMENDMENT 1 - BUILDING CODE OF AUSTRALIA 2022 & HOUSING PROVISIONS STANDARD 2022 & BASIX CERTIFICATE.

MECHANICAL VENTILATION
- EXHAUST FROM A BATHROOM, SANITARY COMPARTMENT TO DISCHARGE DIRECTLY TO OUTDOOR AIR WITH MINIMUM FLOW RATE OF 25L/S & MAKE-UP AIR VIA OPENINGS TO AN ADJACENT ROOM WITH A FREE AREA OF 14,000 MM^2. THIS EXHAUST SYSTEM MUST BE INTERLOCKED WITH LIGHT SWITCH AND INCLUDE RUN-ON TIMER SO THAT THE EXHAUST SYSTEM CONTINUES TO OPERATE FOR 10 MINUTES AFTER THE LIGHT SWITCH IS OFF.
- ANY INSTALLED - KITCHEN RANGEHOOD EXHAUST TO DISCHARGE DIRECTLY OR VIA DUCT TO OUTDOOR AIR WITH MINIMUM FLOW RATE OF 40L/S & MAKE-UP AIR VIA OPENINGS TO AN ADJACENT ROOM WITH A FREE AREA OF 14,000 MM^2.
- LAUNDRY EXHAUST TO DISCHARGE DIRECTLY OR VIA DUCT TO OUTDOOR AIR WITH MINIMUM FLOW RATE OF 40L/S & MAKE-UP AIR VIA OPENINGS TO AN ADJACENT ROOM WITH A FREE AREA OF 14,000 MM^2.





Sydney Wide Certifiers Pty Ltd
Complying Development Certificate
Reference: SWC262403/01
Date: 13/10/2026
Sandres Markhani - BDC05035

HIRA DESIGNS ©
This drawing remains the property of Hira Designs. It may be used for the purpose for which it was commissioned & in accordance with the terms of engagement for that commission.

Rev	Description	Date	App'd
-	CDC DRAWING ISSUED FOR APPROVAL	06.08.26	

Project
PROPOSED DOUBLE STOREY RESIDENCE

7 CATALANA STREET, SPRING FARM 2570
LOT 43, DP1316318

HIRA DESIGNS
Business Address: 13 Feathertop Ave, MINTO NSW 2566
Postal Address: 13 Feathertop Ave, MINTO NSW 2566
Phone Number: 0415112594
Email: info@hiradesigns.com.au
Project Designer:
Pramila Maharjan

Drawing Title
CDC DRAWINGS
BUILDING SPECIFICATION 1

Checked/Approved
PM

Scale
@A3 Sheet Size

Project Number
475041

Drawing Number Revision
CDC-002 -

Status
CDC DRAWINGS


STONEGROVE HOMES

Copyright HIRA DESIGNS ©

Notes
1. CONTRACTOR MUST VERIFY ALL DIMENSIONS ON SITE BEFORE COMMENCING WORK OR PREPARING SHOP DRAWINGS.
2. DO NOT SCALE DRAWINGS.
3. CONTRACTOR TO CHECK UNDERGROUND SERVICES BEFORE COMMENCING WORKS BY CONTACTING DIAL BEFORE YOU DIG. IF DIAL BEFORE YOU DIG INFORMATION IS PROVIDED WITH THIS DOCUMENTATION IT SHALL BE ASSUMED NOT TO BE CURRENT AND CONTRACTOR SHALL MAKE THEIR OWN ENQUIRES.

TERMITE SHEET

- TERMITE SHEET EXTENDS THROUGH THE ENTIRE MASONRY LEAF AND **IS VISIBLE AT THE FINISHED FACE OF THE WALL.**

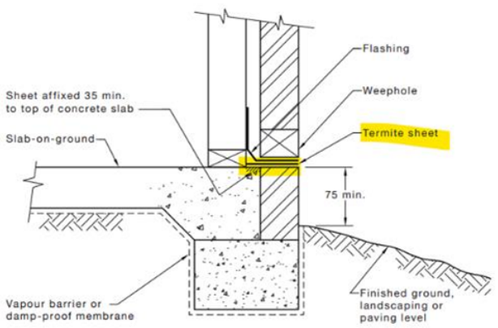


(a) Masonry veneer with separate strip footings


DIMENSIONS IN MILLIMETRES

FIGURE 5.5 (in part) TYPICAL SHEET INSTALLATION TO EXTERNAL WALL WITH CONCRETE FLOOR SLAB

OVERFLOW TO BALCONY:

SURFACE DRAIN & OVERFLOW TO BALCONY

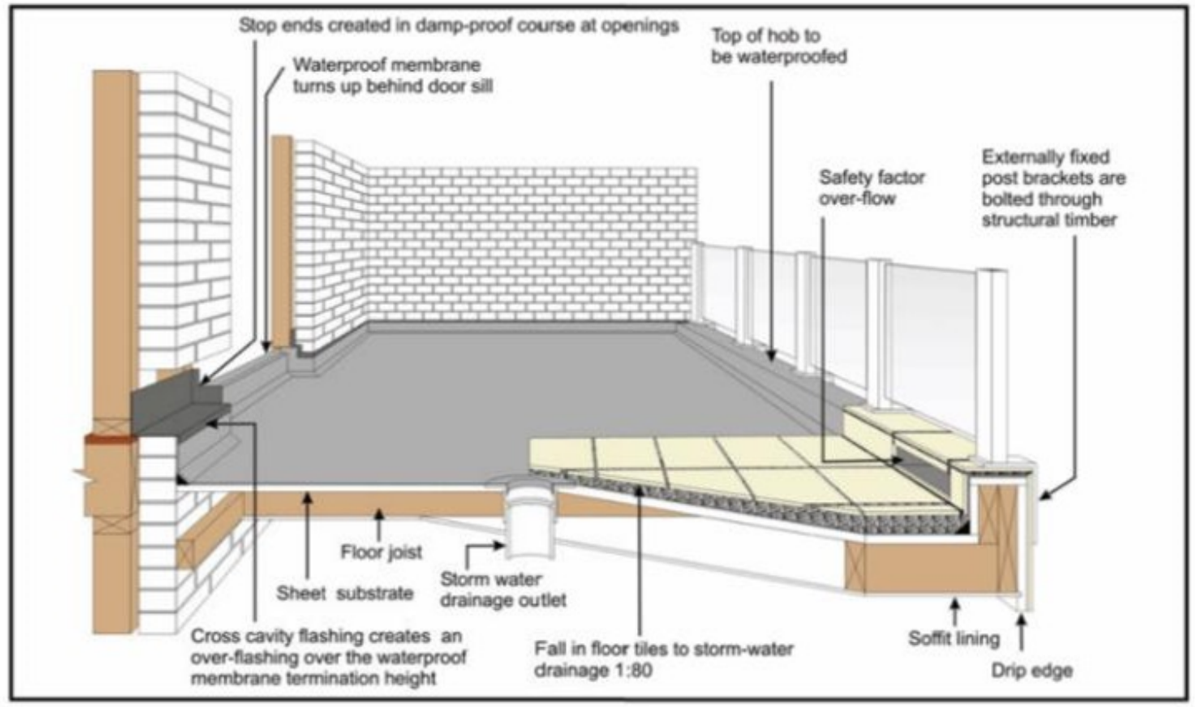

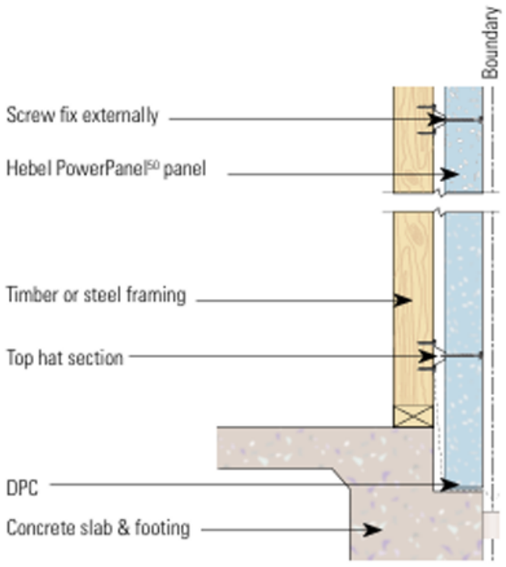

PLANTER BOX

REFER BELOW DETAILS FOR PLANTER BOX.

Sydney Wide Certifiers Pty Ltd
Complying Development Certificate
Reference: SWC262403/01
Date: 13/10/2026
Sandres Markhani BDC05035


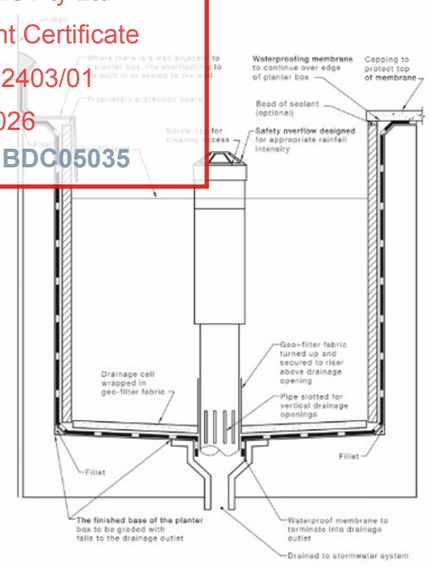


FIGURE 2.17 TYPICAL PLANTER BOX CONSTRUCTION

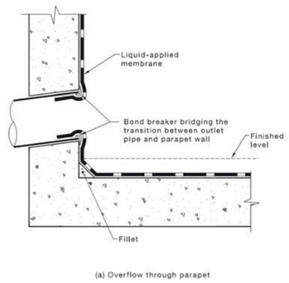

(a) Overflow through parapet

HIRA DESIGNS ©
This drawing remains the property of Hira Designs. It may be used for the purpose for which it was commissioned & in accordance with the terms of engagement for that commission.

Rev	Description	Date	App'd
-	CDC DRAWING ISSUED FOR APPROVAL	06.08.26	

Project
PROPOSED DOUBLE STOREY RESIDENCE

7 CATALANA STREET, SPRING FARM 2570
LOT 43, DP1316318

HIRA DESIGNS
Business Address: 13 Feathertop Ave, MINTO NSW 2566
Postal Address: 13 Feathertop Ave, MINTO NSW 2566
Phone Number: 0415112594
Email: info@hiradesigns.com.au
Project Designer:
Pramila Maharjan

Drawing Title
CDC DRAWINGS
BUILDING SPECIFICATION 2

Checked/Approved
PM

Scale
@A3 Sheet Size

Project Number
475041

Drawing Number Revision
CDC-003 -

Status
CDC DRAWINGS

STONEGROVE HOMES

Copyright HIRA DESIGNS ©

Notes
1. CONTRACTOR MUST VERIFY ALL DIMENSIONS ON SITE BEFORE COMMENCING WORK OR PREPARING SHOP DRAWINGS.
2. DO NOT SCALE DRAWINGS.
3. CONTRACTOR TO CHECK UNDERGROUND SERVICES BEFORE COMMENCING WORKS BY CONTACTING DIAL BEFORE YOU DIG. IF DIAL BEFORE YOU DIG INFORMATION IS PROVIDED WITH THIS DOCUMENTATION IT SHALL BE ASSUMED NOT TO BE CURRENT AND CONTRACTOR SHALL MAKE THEIR OWN ENQUIRES.

WATERPROOFING

FALL TO FLOOR WASTE TO BE **MINIMUM 1:80 TO MAXIMUM 1:50**

Figure 10.2.29: Typical membrane termination at drainage outlet



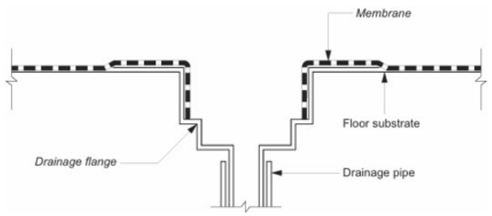


Figure 10.2.24: Typical bathroom door details for whole bathroom waterproofing

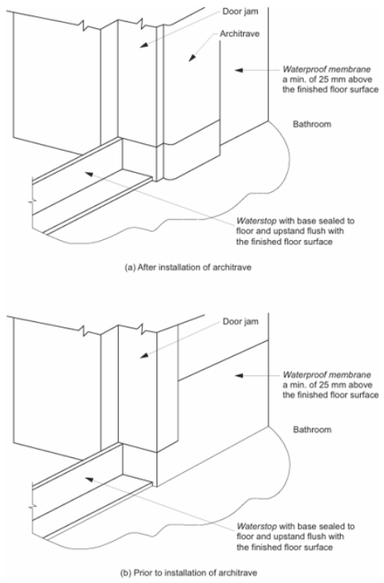

BASIN & BATHTUB


Figure 10.2.5: Bath and vessel abutting wall — areas to be protected

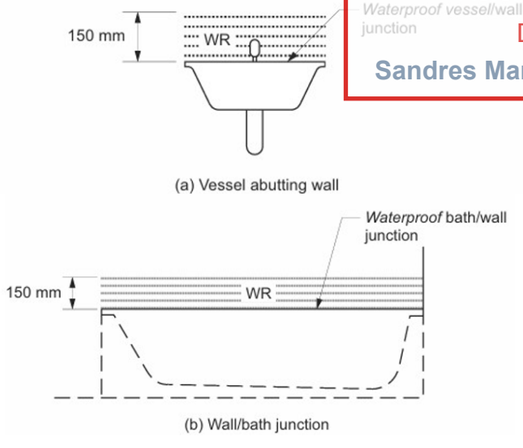


Sydney Wide Certifiers Pty Ltd
Complying Development Certificate
Reference: SWC262403/01
Date: 13/10/2026
Sandres Markhani BDC05035

ENCLOSED SHOWER AREA

Figure 10.2.17: Typical hobless construction

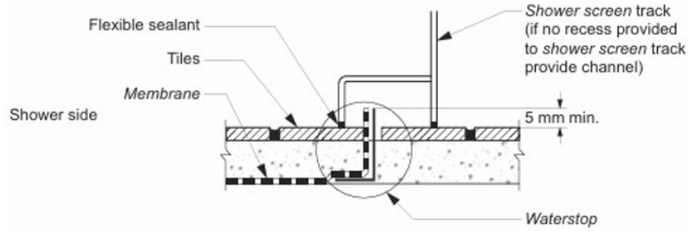

Extent of treatment for shower areas — concrete compressed fibre-cement and fibre-cement sheet floors

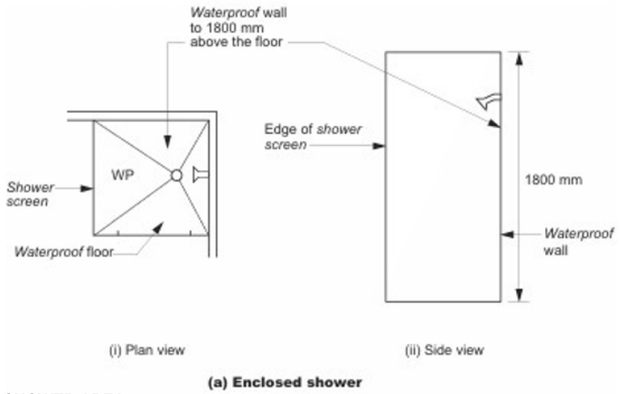

UNENCLOSED SHOWER AREA


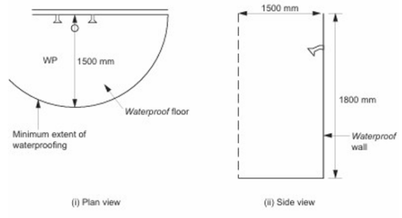


Figure 10.2.18: Typical termination of membrane at extent of shower area

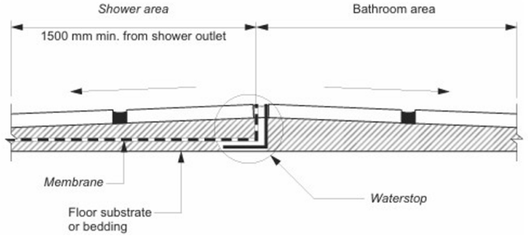

Rev	Description	Date	App'd
-	CDC DRAWING ISSUED FOR APPROVAL	06.08.26	

Project
PROPOSED DOUBLE STOREY RESIDENCE

7 CATALANA STREET, SPRING FARM 2570
LOT 43, DP1316318

HIRA DESIGNS
Business Address: 13 Feathertop Ave, MINTO NSW 2566
Postal Address: 13 Feathertop Ave, MINTO NSW 2566
Phone Number: 0415112594
Email: info@hiradesigns.com.au
Project Designer:
Pramila Maharjan

Drawing Title
CDC DRAWINGS
BUILDING SPECIFICATION 3

Checked/Approved
PM

Scale
@A3 Sheet Size

Project Number
475041

Drawing Number Revision
CDC-004 -


Status
CDC DRAWINGS

STONEGROVE HOMES

HIRA DESIGNS ©
This drawing remains the property of Hira Designs. It may be used for the purpose for which it was commissioned & in accordance with the terms of engagement for that commission.

Copyright HIRA DESIGNS ©

Notes
1. CONTRACTOR MUST VERIFY ALL DIMENSIONS ON SITE BEFORE COMMENCING WORK OR PREPARING SHOP DRAWINGS.
2. DO NOT SCALE DRAWINGS.
3. CONTRACTOR TO CHECK UNDERGROUND SERVICES BEFORE COMMENCING WORKS BY CONTACTING DIAL BEFORE YOU DIG. IF DIAL BEFORE YOU DIG INFORMATION IS PROVIDED WITH THIS DOCUMENTATION IT SHALL BE ASSUMED NOT TO BE CURRENT AND CONTRACTOR SHALL MAKE THEIR OWN ENQUIRES.

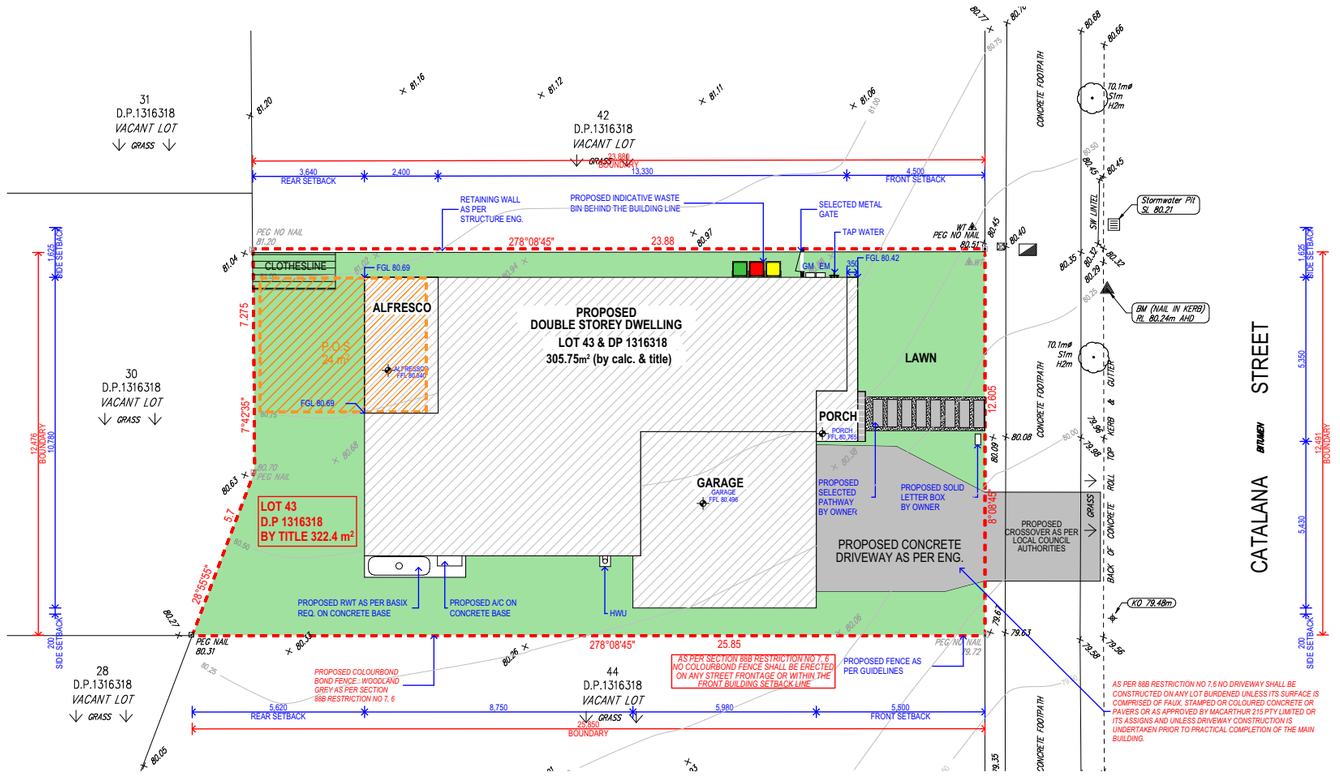

PROPOSED SITE PLAN 1:200

Sydney Wide Certifiers Pty Ltd
Complying Development Certificate
Reference: SWC262403/01
Date: 13/10/2026
Sandres Markhani BDC05035

AS PER 88B RESTRICTION NO 7

4. NO BUILDING OR BUILDINGS SHALL BE ERECTED OR BE PERMITTED TO REMAIN ERECTED ON ANY LOT BURDENED OTHER THAN WITH EXTERNAL WALLS OF BRICK AND/OR BRICK VENEER AND/OR STONE AND/OR CONCRETE AND/OR GLASS AND/OR TIMBER AND/OR HARDIPLANK OR SIMILAR PRODUCT. NO BUILDING OR BUILDINGS SHALL BE ERECTED OR BE PERMITTED TO REMAIN ERECTED ON ANY LOT BURDENED HAVING A ROOF OTHER THAN CLAY TILES, CEMENT TILES, SLATE OR NON REFTECTIVE SURFACE CORRUGATED IRON. ALL ROOFING MATERIALS SHALL BE NEUTRAL COLOURS OR SHADES OF GREY.

6. NO FENCE SHALL BE ERECTED OR PERMITTED TO REMAIN ON ANY LOT HEREBY BURDENED UNLESS THE SAME IS OF LAPPED AND CAPPED CONSTRUCTION OR COLORBOND FENCE PROVIDED THAT COLORBOND FENCE CAN ONLY USE COLOURS, SHALE GREY, DUNE, BASALT OR WOODLAND GREY.

8.NO ADVERTISING HOARDING SIGNS OR MATTER SHALL BE DISPLAYED OR ERECTED ON ANY LOT BURDENED (OTHER THAN A SIGN ADVERTISING THAT THE SAID LOT IS FOR SALE) WITHOUT THE PRIOR WRITTEN CONSENT OF MACARTHUR 215 PTY LIMITED OR ITS SUCCESSORS IN TITLE OR ASSIGNS.

9. NO DRIVEWAY SHALL BE CONSTRUCTED ON ANY LOT BURDENED UNLESS ITS SURFACE IS COMPRISED OF FAUX, STAMPED OR COLOURED CONCRETE OR PAVERS OR AS APPROVED BY MACARTHUR 215 PTY LIMITED OR ITS ASSIGNS AND UNLESS DRIVEWAY CONSTRUCTION IS UNDERTAKEN PRIOR TO PRACTICAL COMPLETION OF THE MAIN BUILDING

10. NO DWELLING SHALL BE ERECTED OR PERMITTED TO REMAIN ON ANY LOT BURDENED UNLESS ARE BETWEEN THE BUILDING AND THE BOUNDARY OF THE LOT BURDENED IS TURFED..

AS PER 88B RESTRICTION NO 10

NO DEVELOPMENT INCLUDING EARTHWORKS, BUILDINGS, FOOTINGS/FOUNDATIONS AND ASSOCIATED INFRASTRUCTURE SHALL BE CARRIED OUT OR CONSTRUCTED ON THE LOTS HEREBY BURDENED UNLESS HAVE BEEN DESIGNED BY A QUALIFIED CIVIL/STRUCTURAL ENGINEER BASED ON GEO-TECHNICAL ADVICE FROM A QUALIFIED GEOTECHNICAL CONSULTANT.

AS PER 88B RESTRICTION NO 12

NO DEVELOPMENT WORKS INCLUDING EARTHWORKS, IMPORTED FILL, LANDSCAPING, ROADS, BUILDINGS, AND ASSOCIATED INFRASTRUCTURE SHALL BE CARRIED OUT OR CONSTRUCTED ON THE LOTS HEREBY BURDENED UNLESS IN ACCORDANCE WITH THE MANAGEMENT STRATEGIES AS CONTAINED WITHIN THE REPORT TITLED - POST-CONSTRUCTION SALINITY

General Notes:

- Design to comply with Building Code of Australia (BCA) 2022 and subsequent amendments.
- All glazing will be installed in accordance with AS 1288 (Glass in buildings - Selection and Installation).
- All treads, internal or external, or nosing's of a stairway to comply with slip-resistance classification of (AS 4586-2013 & BCA 2022)
- Proposed brick cavity wall to be 60/60/60 Fire Wall in accordance with Part 9.3.1 and Sound Insulation requirements in accordance with Part 10.7.1 of BCA 2022".
- Smoke Alarm to be located and interconnected with each other in accordance with Part 9.5.2 and 9.5.4 of BCA 2022".
- Rainwater tank capacity as specified in the basix certificate accompanying the proposal.
- Window Schedule complying with BASIX Certificate requirements.
- Restriction of openable part of windows to 125mm where the floor level of a bedroom window is more than 2 metres above ground level.
- Timber framing to be as per AS 1684
- Balustrade height to be minimum 1000mm.
- Stairway clearanceto be minimum 2000mm.
- The door to a fully enclosed sanitary compartment will open outwards, slide or be readily removable from the outside of the compartment, where a clear space of at least 1.2m is provided between the closet pan within the sanitary compartment and the nearest part of the doorway.
- All electrical, mechanical, hydraulic and air conditioning equipment to be housed so that it does not create an "Offensive Noise" as defined in the Protection of the Environment Operations Act 1997 either within or at the boundaries of any property at any time of the day.
- All lots must have access to reticulated water, sewer, electricty, telecommunications and gas where available

HIRA DESIGNS ©
This drawing remains the property of Hira Designs. It may be used for the purpose for which it was commissioned & in accordance with the terms of engagement for that commission.

Rev	Description	Date	App'd
-	CDC DRAWING ISSUED FOR APPROVAL	06.08.26	

Project
PROPOSED DOUBLE STOREY RESIDENCE

7 CATALANA STREET, SPRING FARM 2570
LOT 43, DP1316318

HIRA DESIGNS
Business Address: 13 Feathertop Ave, MINTO NSW 2566
Postal Address: 13 Feathertop Ave, MINTO NSW 2566
Phone Number: 0415112594
Email: info@hiradesigns.com.au
Project Designer:
Pramila Maharjan

Drawing Title
CDC DRAWINGS
SITE PLAN

Checked/Approved
PM

Scale
@A3 Sheet Size

Project Number
475041


Drawing Number Revision
CDC-100 -

Status
CDC DRAWINGS

STONEGROVE HOMES

Copyright HIRA DESIGNS ©

Notes
1. CONTRACTOR MUST VERIFY ALL DIMENSIONS ON SITE BEFORE COMMENCING WORK OR PREPARING SHOP DRAWINGS.
2. DO NOT SCALE DRAWINGS.
3. CONTRACTOR TO CHECK UNDERGROUND SERVICES BEFORE COMMENCING WORKS BY CONTACTING DIAL BEFORE YOU DIG. IF DIAL BEFORE YOU DIG INFORMATION IS PROVIDED WITH THIS DOCUMENTATION IT SHALL BE ASSUMED NOT TO BE CURRENT AND CONTRACTOR SHALL MAKE THEIR OWN ENQUIRES.

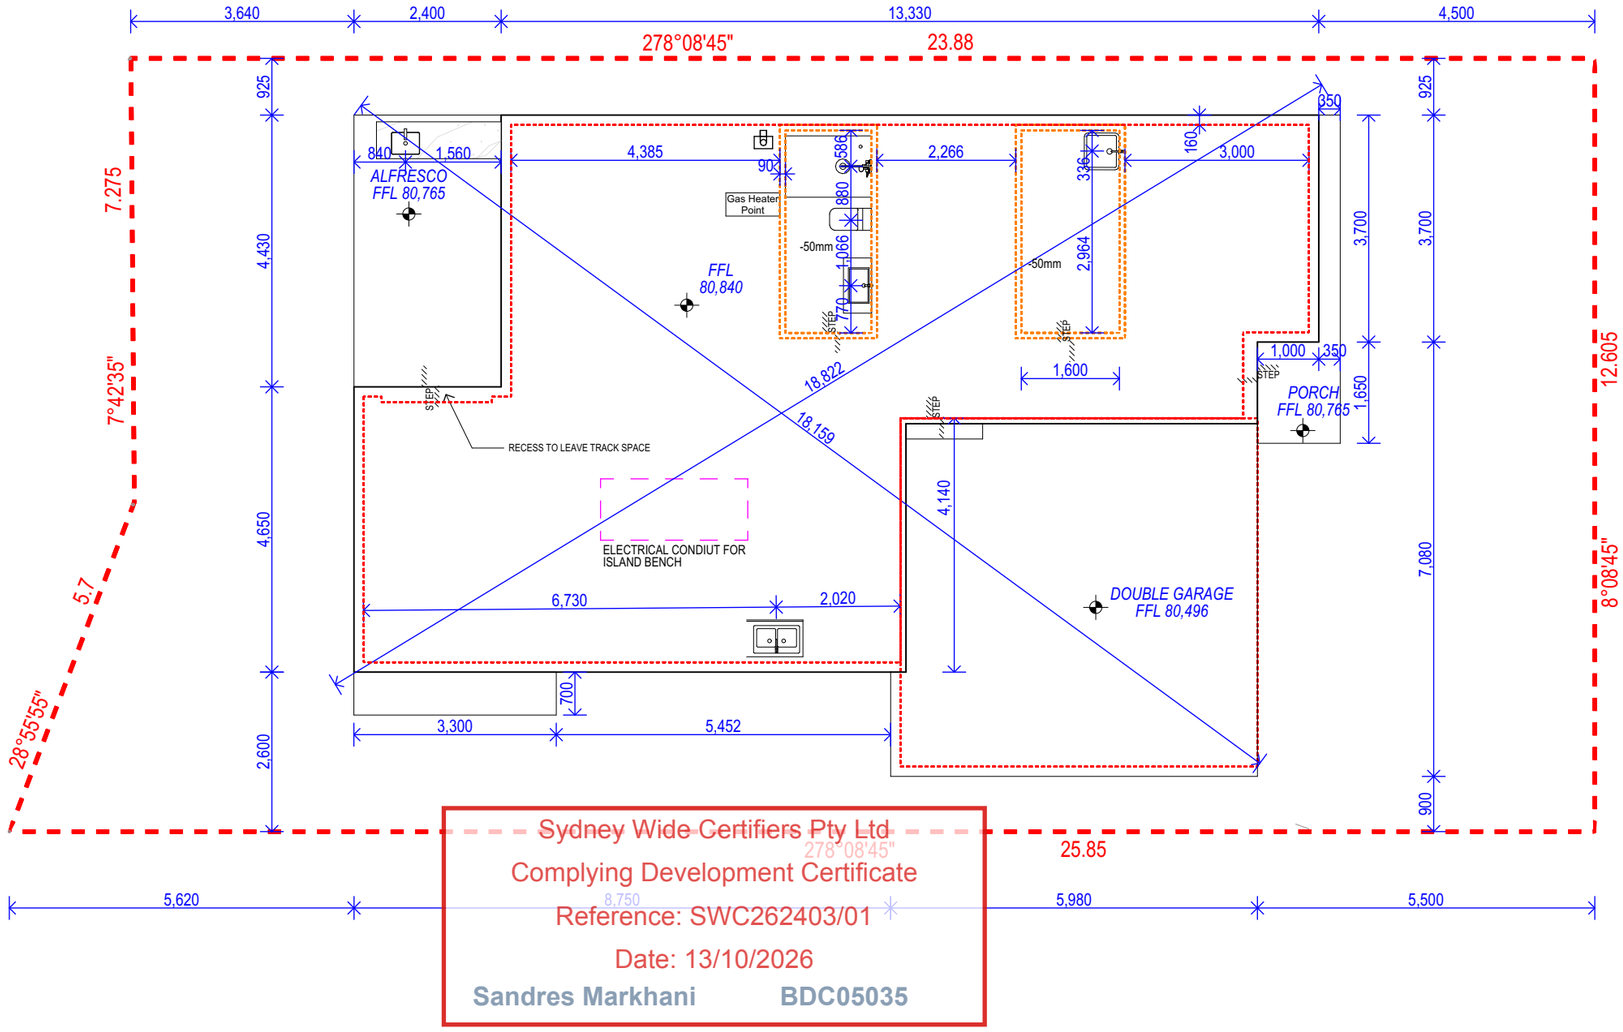

Sydney Wide Certifiers Pty Ltd
Complying Development Certificate
Reference: SWC262403/01
Date: 13/10/2026
Sandres Markhani BDC05035

SLAB PLAN 1:100

Rev	Description	Date	App'd
-	CDC DRAWING ISSUED FOR APPROVAL	06.08.26	

Project
PROPOSED DOUBLE STOREY RESIDENCE

7 CATALANA STREET, SPRING FARM 2570
LOT 43, DP1316318

HIRA DESIGNS
Business Address: 13 Feathertop Ave, MINTO NSW 2566
Postal Address: 13 Feathertop Ave, MINTO NSW 2566
Phone Number: 0415112594
Email: info@hiradesigns.com.au
Project Designer:
Pramila Maharjan

Drawing Title
CDC DRAWINGS
SLAB PLAN

Checked/Approved
PM

Scale
1:100 @A3 Sheet Size

Project Number
475041

Drawing Number Revision
CDC-101 -


Status
CDC DRAWINGS

STONEGROVE HOMES

HIRA DESIGNS ©
This drawing remains the property of Hira Designs. It may be used for the purpose for which it was commissioned & in accordance with the terms of engagement for that commission.

Copyright HIRA DESIGNS ©

Notes
1. CONTRACTOR MUST VERIFY ALL DIMENSIONS ON SITE BEFORE COMMENCING WORK OR PREPARING SHOP DRAWINGS.
2. DO NOT SCALE DRAWINGS.
3. CONTRACTOR TO CHECK UNDERGROUND SERVICES BEFORE COMMENCING WORKS BY CONTACTING DIAL BEFORE YOU DIG. IF DIAL BEFORE YOU DIG INFORMATION IS PROVIDED WITH THIS DOCUMENTATION IT SHALL BE ASSUMED NOT TO BE CURRENT AND CONTRACTOR SHALL MAKE THEIR OWN ENQUIRES.

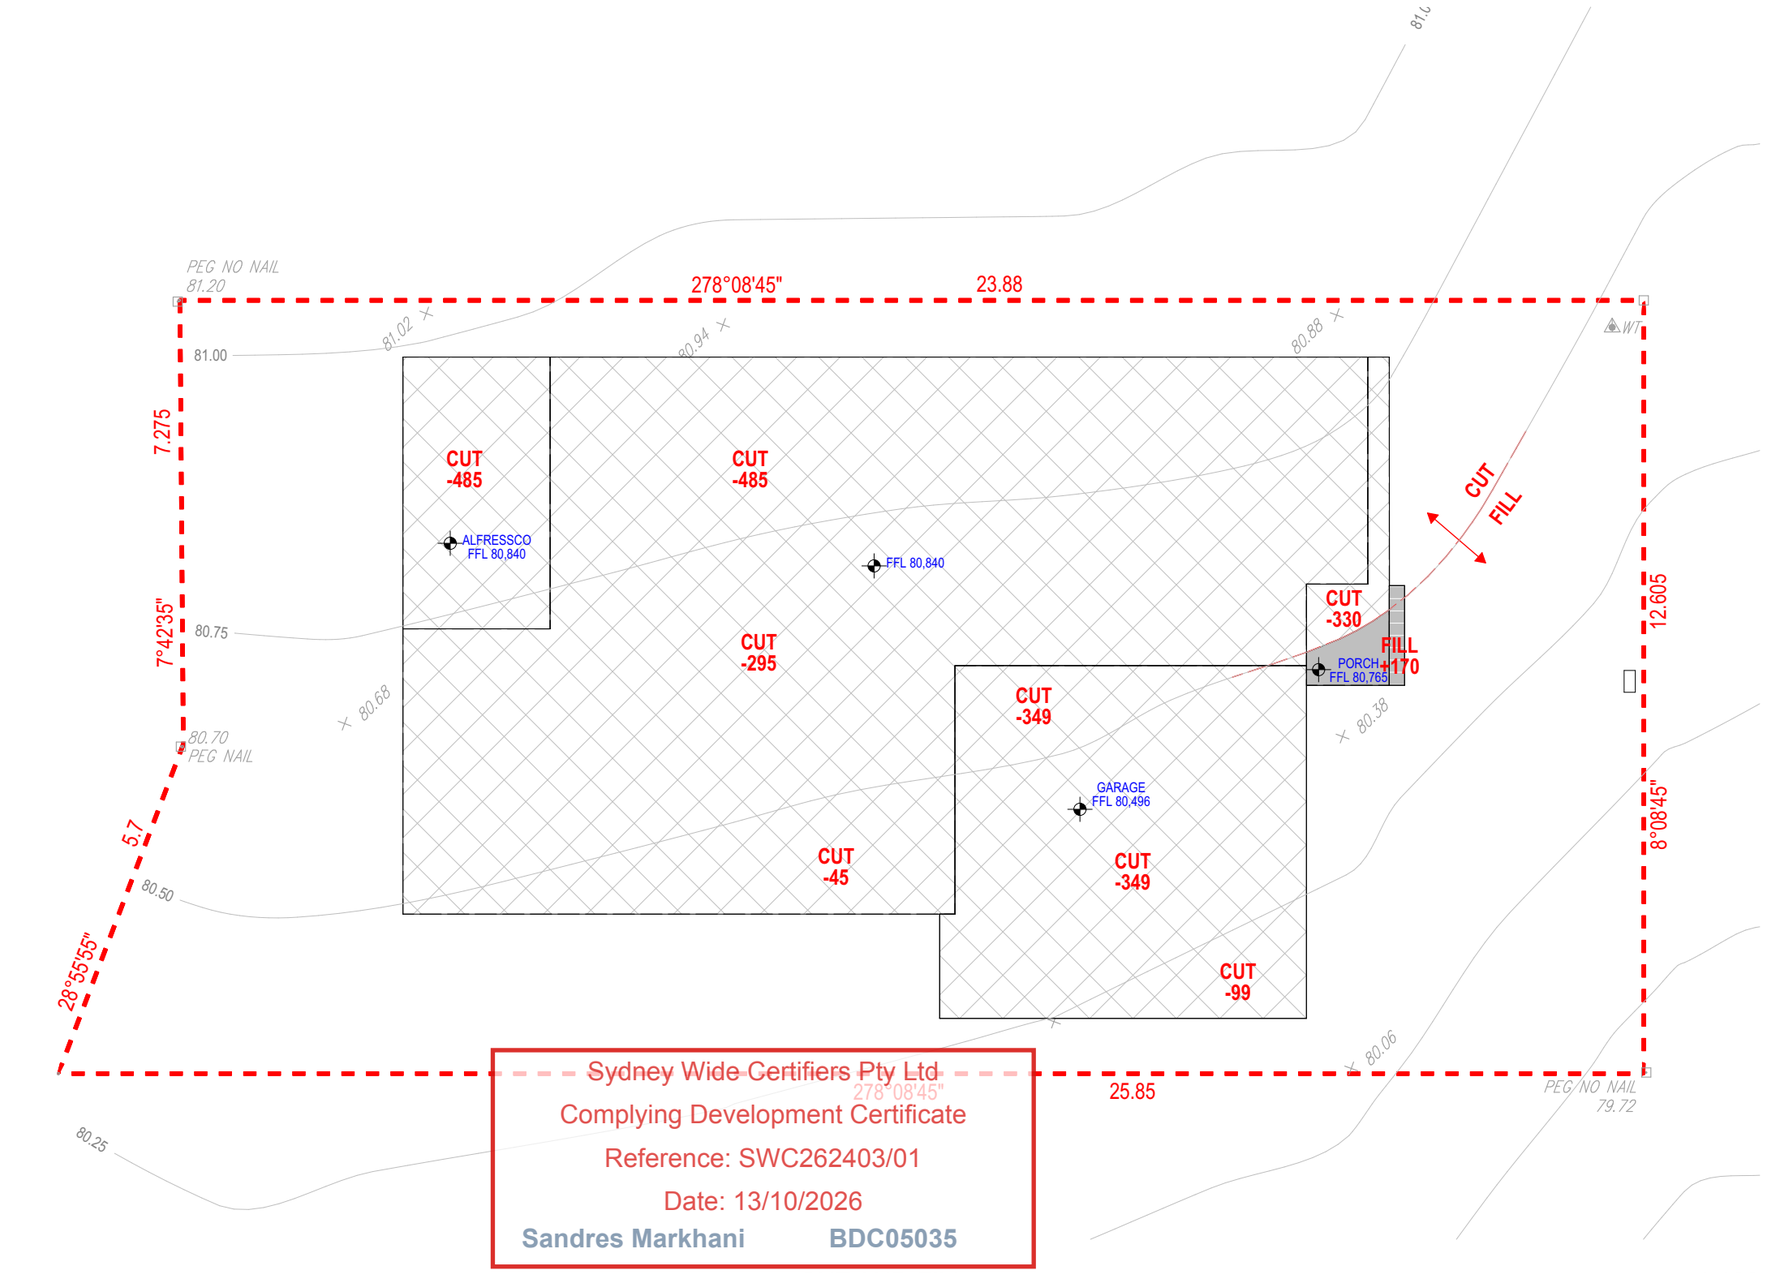

CUT AND FILL 1:100

Rev	Description	Date	App'd
-	CDC DRAWING ISSUED FOR APPROVAL	06.08.26	

Project
PROPOSED DOUBLE STOREY RESIDENCE

7 CATALANA STREET, SPRING FARM 2570
LOT 43, DP1316318

HIRA DESIGNS
Business Address: 13 Feathertop Ave, MINTO NSW 2566
Postal Address: 13 Feathertop Ave, MINTO NSW 2566
Phone Number: 0415112594
Email: info@hiradesigns.com.au

Project Designer:
Pramila Maharjan

Drawing Title
CDC DRAWINGS
CUT & FILL

Checked/Approved
PM

Scale
1:100 @A3 Sheet Size

Project Number
475041

Drawing Number Revision
CDC-102 -


Status
CDC DRAWINGS

STONEGROVE HOMES

HIRA DESIGNS ©
This drawing remains the property of Hira Designs. It may be used for the purpose for which it was commissioned & in accordance with the terms of engagement for that commission.

Copyright HIRA DESIGNS ©

Notes
1. CONTRACTOR MUST VERIFY ALL DIMENSIONS ON SITE BEFORE COMMENCING WORK OR PREPARING SHOP DRAWINGS.
2. DO NOT SCALE DRAWINGS.
3. CONTRACTOR TO CHECK UNDERGROUND SERVICES BEFORE COMMENCING WORKS BY CONTACTING DIAL BEFORE YOU DIG. IF DIAL BEFORE YOU DIG INFORMATION IS PROVIDED WITH THIS DOCUMENTATION IT SHALL BE ASSUMED NOT TO BE CURRENT AND CONTRACTOR SHALL MAKE THEIR OWN ENQUIRES.

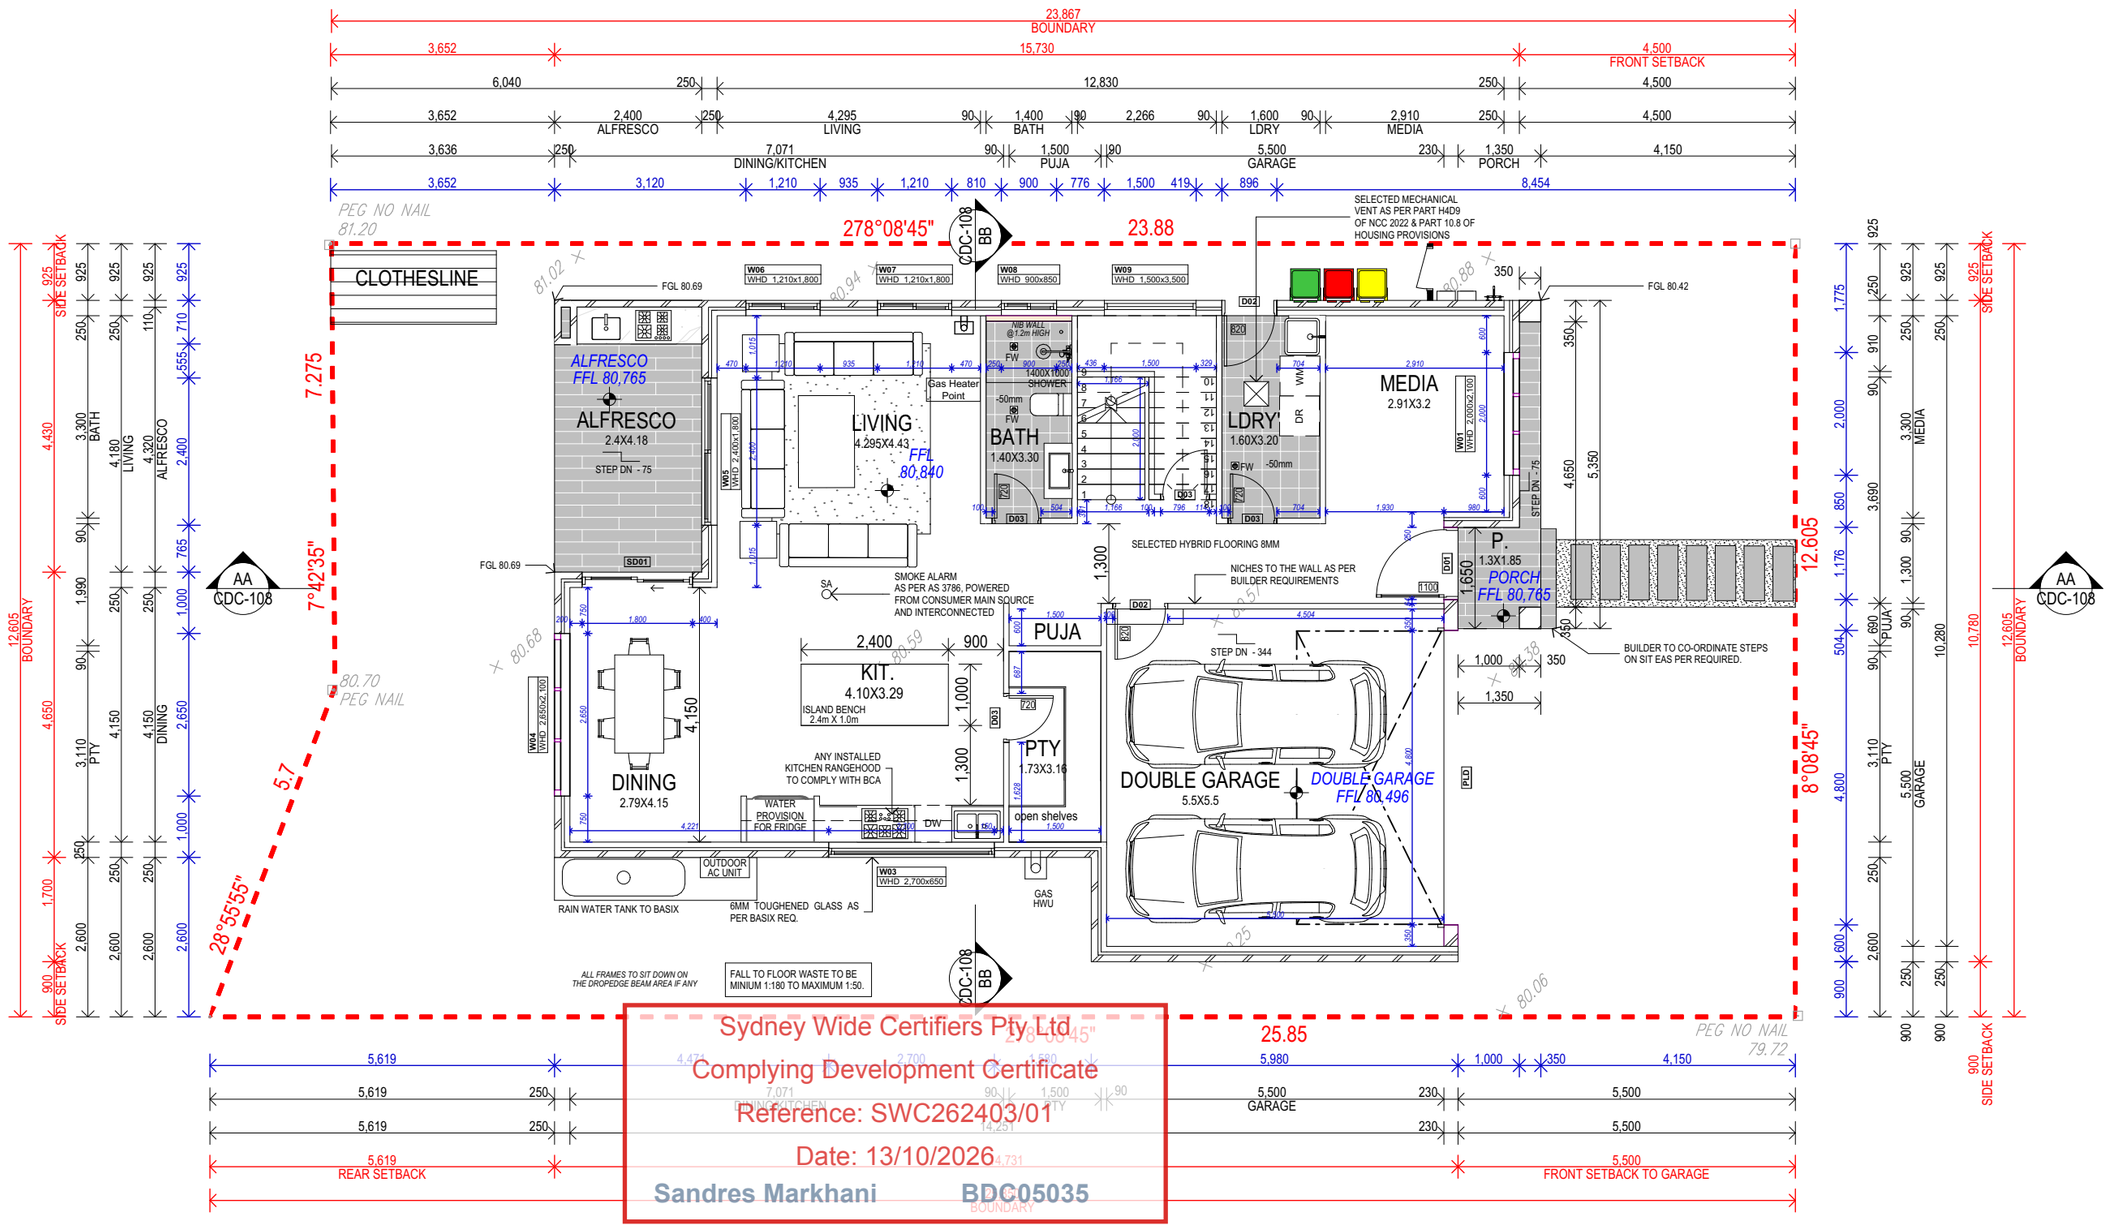

Sydney Wide Certifiers Pty Ltd
Complying Development Certificate
Reference: SWC262403/01
Date: 13/10/2026
Sandres Markhani BDC05035

GROUND FLOOR PLAN

1:100

AS PER 88B RESTRICTION NO 7
4.NO BUILDING OR BUILDINGS SHALL BE ERECTED OR BE PERMITTED TO REMAIN ERECTED ON ANY LOT BURDENED OTHER THAN WITH EXTERNAL WALLS OF BRICK AND/OR BRICK VENEER AND/OR STONE AND/OR CONCRETE AND/OR GLASS AND/OR TIMBER AND/OR HARDIPLANK OR SIMILAR PRODUCT. NO BUILDING OR BUILDINGS SHALL BE ERECTED OR PERMITTED TO REMAIN ERECTED ON ANY LOT BURDENED HAVING A ROOF OTHER THAN CLAY TILES, CEMENT TILES, SLATE OR NON REFTECTIVE SURFACE CORRUGATED IRON. ALL ROOFING MATERIALS SHALL BE NEUTRAL COLOURS OR SHADES OF GREY.
6.NO FENCE SHALL BE ERECTED OR PERMITTED TO REMAIN ON ANY LOT HEREBY BURDENED UNLESS THE FENCING IS OF A TIMBER LAPPED AND/OR LAPPED AND CAPPED CONSTRUCTION OR COLORBOND FENCE PROVIDED THAT COLORBOND FENCE CAN ONLY USE COLOURS, SHALE GREY, DUNE, BASALT OR WOODLAND GREY.
8.NO ADVERTISING HOARDING SIGNS OR MATTER SHALL BE DISPLAYED OR ERECTED ON ANY LOT BURDENED (OTHER THAN A SIGN ADVERTISING THAT THE SAID LOT IS FOR SALE) WITHOUT THE PRIOR WRITTEN CONSENT OF MACARTHUR 215 PTY LIMITED OR ITS SUCCESSORS IN TITLE OR ASSIGNS.
9.NO DRIVEWAY SHALL BE CONSTRUCTED ON ANY LOT BURDENED UNLESS ITS SURFACE IS COMPRISED OF FAUX, STAMPED OR COLOURED CONCRETE OR PAVERS OR AS APPROVED BY MACARTHUR 215 PTY LIMITED OR ITS ASSIGNS AND UNLESS DRIVEWAY CONSTRUCTION IS UNDERTAKEN PRIOR TO PRACTICAL COMPLETION OF THE MAIN BUILDING.
10.NO DWELLING SHALL BE ERECTED OR PERMITTED TO REMAIN ON ANY LOT BURDENED UNLESS THE AREA BETWEEN THE BUILDING LINE AND THE FRONT BOUNDARY OF THE LOT BURDENED IS TURFED.
AS PER 88B RESTRICTION NO 10
NO DEVELOPMENT INCLUDING EARTHWORKS, BUILDINGS, FOOTINGS/FOUNDATIONS AND ASSOCIATED INFRASTRUCTURE SHALL BE CARRIED OUT OR CONSTRUCTED ON THE LOTS HEREBY BURDENED UNLESS HAVE BEEN DESIGNED BY A QUALIFIED CIVIL/STRUCTURAL ENGINEER BASED ON GEO-TECHNICAL ADVICE FROM A QUALIFIED GEOTECHNICAL CONSULTANT.
AS PER 88B RESTRICTION NO 12
NO DEVELOPMENT WORKS INCLUDING EARTHWORKS, IMPORTED FILL, LANDSCAPING, ROADS, BUILDINGS, AND ASSOCIATED INFRASTRUCTURE SHALL BE CARRIED OUT OR CONSTRUCTED ON THE LOTS HEREBY BURDENED UNLESS IN ACCORDANCE WITH THE MANAGEMENT STRATEGIES AS CONTAINED WITHIN THE REPORT TITLED - POST-CONSTRUCTION SALINITY

WATERPROOFING TO ALL WET AREAS NEEDS TO BE EITHER COMPLY WITH PART 10.2 OF THE ABCB HOUSING PROVISIONS STANDARD 2022 (BCA) OR AS 3740.2021 & 10.2.1 TO 10.2.6 AND 10.2.12 OF THE ABCB HOUSING PROVISIONS STANDARD 2022.

WET AREAS: FALL TO FLOOR WASTE TO BE MINIMUM 1:80 TO MAXIMUM 1:50.

GENERAL NOTES:
•BUILDER TO PROVIDE SLAB UNDER RWT, AC OUTDOOR UNIT & BINS AREA
•BUILDER TO PROVIDE PROVISION FOR DISHWASHER, LAUNDRY MACHINE, DRYER, FRIDGE & TV
•BUILDER TO PROVIDE PROVISION OF WATER CONNECTION IN FRIDGE SPACE •KITCHEN RANGEHOOD DUCTED TO FACADE AND TO COMPLY WITH REQUIREMNTS OF NCC
•ALL ROBES IN THE BEDROOM 600mm DEEP, UNLESS OTHERWISE NOTED
•STAIR RISERS, TREADS & BALUSTRADES TO COMPLY WITH REQUIREMNTS OF NCC •ALL STAIRS STRUCTURE TO STRUCTURAL ENGINEERS DETAILS AND AS PER NCC PART 11.2
•BALUSTRADES AS REQUIRED TO STRUCTURAL ENG'S DETAILS & NCC REQUIREMENTS

•LOCATIONS OF MECH. VENTS, SMOKE ALARMS & FLOOR WASTE SHOWN ON PLANS IS INDICATIVE ONLY. BUILDER TO CORDINATE ON SITE AND COMPLY WITH NCC & RELEVANT AUS. STANDARDS
•SMOKE ALARM IN ACCORDANCE WITH NCC PART 9.5.2, 9.5.4 & AS3786 •SMOKE ALARM POWDERED FROM CONSUMER MAINS SOURCE AND INTERCONNECTED •ALL WET AREAS TO COMPLY WITH NCC PART 10.2 & AS3740
•EXHAUST FROM ALL BATHROOMS/SANITARY COMPARTMENT, KITCHEN & LAUNDRY TO COMPLY WITH NCC PART 10.8. THEY NEED TO DISCHARGE DIRECTLY TO OUTDOOR AIR/EXTERNALLY DUCTED.
•THIS EXHAUST SYSTEM MUST BE INTERLOCKED WITH ROOM'S LIGHT SWITCH AND INCLUDE A RUN-ON TIMER SO THAT THE EXHAUST SYSTEM CONTINUES TO OPERATE FOR 10 MINUTES AFTER THE LIGHT SWITCH IS OFF.

WALL TYPES:
EXTERNAL WALLS: BRICK (110mm) + INSULATION TO BASIX + ONE LAYER OF 10MM STANDARD PLASTERBOARD SCREW FIXED TO TIMBER FRAME SPACED AS PER MANUFACTURE DETAIL INTERNAL WALLS: 10MM PLASTERBOARD SCREW FIXED TO TIMBER STUD FRAME

HIRA DESIGNS ©
This drawing remains the property of Hira Designs. It may be used for the purpose for which it was commissioned & in accordance with the terms of engagement for that commission.

Rev	Description	Date	App'd
-	CDC DRAWING ISSUED FOR APPROVAL	06.08.26	

Project
PROPOSED DOUBLE STOREY RESIDENCE
7 CATALANA STREET, SPRING FARM 2570
LOT 43, DP1316318

HIRA DESIGNS
Business Address: 13 Feathertop Ave, MINTO NSW 2566
Postal Address: 13 Feathertop Ave, MINTO NSW 2566
Phone Number: 0415112594
Email: info@hiradesigns.com.au
Project Designer:
Pramila Maharjan

Drawing Title
CDC DRAWINGS
GROUND FLOOR PLAN

Checked/Approved
PM

Scale
1:100 @A3 Sheet Size

Project Number
475041


Drawing Number Revision
CDC-103 -

Status
CDC DRAWINGS

STONEGROVE HOMES

Copyright HIRA DESIGNS ©

Notes
1. CONTRACTOR MUST VERIFY ALL DIMENSIONS ON SITE BEFORE COMMENCING WORK OR PREPARING SHOP DRAWINGS.
2. DO NOT SCALE DRAWINGS.
3. CONTRACTOR TO CHECK UNDERGROUND SERVICES BEFORE COMMENCING WORKS BY CONTACTING DIAL BEFORE YOU DIG. IF DIAL BEFORE YOU DIG INFORMATION IS PROVIDED WITH THIS DOCUMENTATION IT SHALL BE ASSUMED NOT TO BE CURRENT AND CONTRACTOR SHALL MAKE THEIR OWN ENQUIRES.

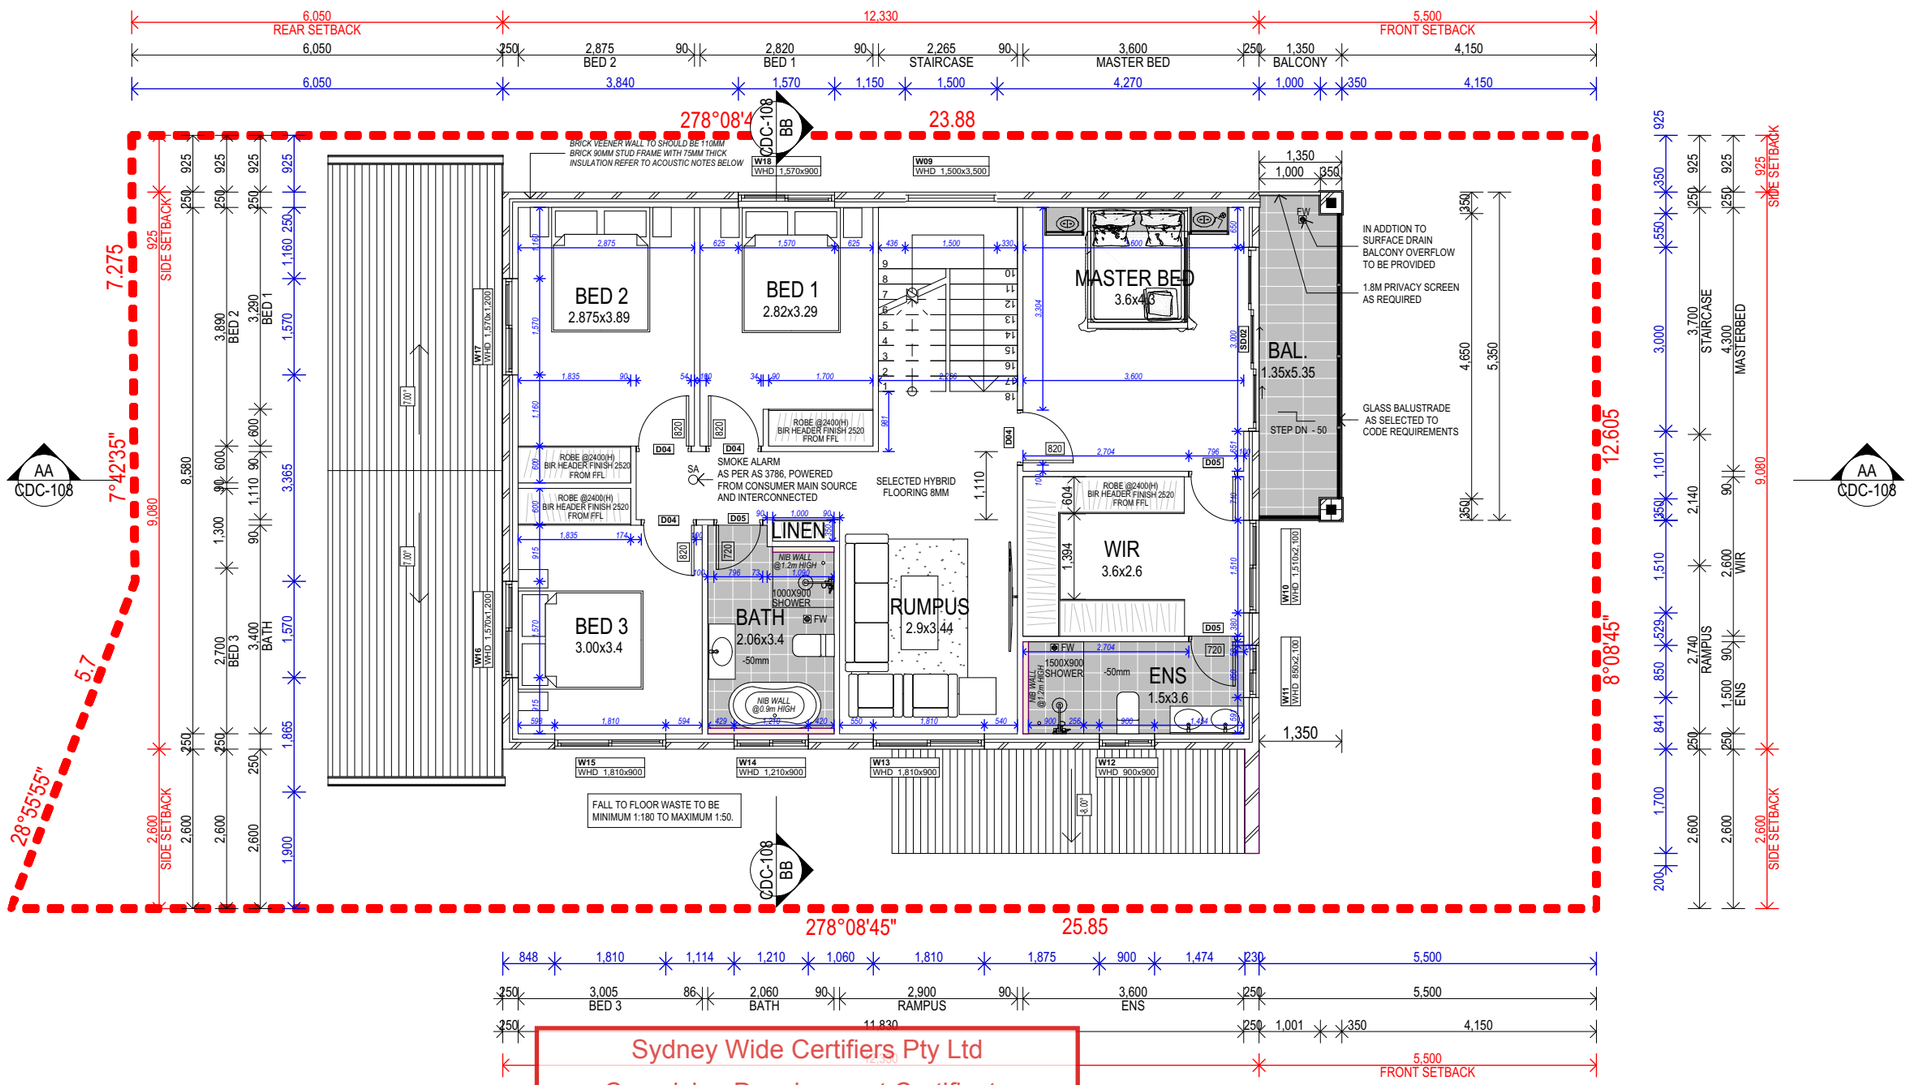

Sydney Wide Certifiers Pty Ltd
Complying Development Certificate
Reference: SWC262403/01
Date: 13/10/2026
Sandres Markhani BDC05035

FIRST FLOOR PLAN

1:100

AS PER 88B RESTRICTION NO 7
4.NO BUILDING OR BUILDINGS SHALL BE ERECTED OR BE PERMITTED TO REMAIN ERECTED ON ANY LOT BURDENED OTHER THAN WITH EXTERNAL WALLS OF BRICK AND/OR BRICK VENEER AND/OR STONE AND/OR CONCRETE AND/OR GLASS AND/OR TIMBER AND/OR HARDIPLANK OR SIMILAR PRODUCT. NO BUILDING OR BUILDINGS SHALL BE ERECTED OR PERMITTED TO REMAIN ERECTED ON ANY LOT BURDENED HAVING A ROOF OTHER THAN CLAY TILES, CEMENT TILES, SLATE OR NON REFTECTIVE SURFACE CORRUGATED IRON. ALL ROOFING MATERIALS SHALL BE NEUTRAL COLOURS OR SHADES OF GREY.
6.NO FENCE SHALL BE ERECTED OR PERMITTED TO REMAIN ON ANY LOT HEREBY BURDENED UNLESS THE FENCING IS OF A TIMBER LAPPED AND/OR LAPPED AND CAPPED CONSTRUCTION OR COLORBOND FENCE PROVIDED THAT COLORBOND FENCE CAN ONLY USE COLOURS, SHALE GREY, DUNE, BASALT OR WOODLAND GREY.
8.NO ADVERTISING HOARDING SIGNS OR MATTER SHALL BE DISPLAYED OR ERECTED ON ANY LOT BURDENED (OTHER THAN A SIGN ADVERTISING THAT THE SAID LOT IS FOR SALE) WITHOUT THE PRIOR WRITTEN CONSENT OF MACARTHUR 215 PTY LIMITED OR ITS SUCCESSORS IN TITLE OR ASSIGNS.
9.NO DRIVEWAY SHALL BE CONSTRUCTED ON ANY LOT BURDENED UNLESS ITS SURFACE IS COMPRISED OF FAUX, STAMPED OR COLOURED CONCRETE OR PAVERS OR AS APPROVED BY MACARTHUR 215 PTY LIMITED OR ITS ASSIGNS AND UNLESS DRIVEWAY CONSTRUCTION IS UNDERTAKEN PRIOR TO PRACTICAL COMPLETION OF THE MAIN BUILDING.
10.NO DWELLING SHALL BE ERECTED OR PERMITTED TO REMAIN ON ANY LOT BURDENED UNLESS THE AREA BETWEEN THE BUILDING LINE AND THE FRONT BOUNDARY OF THE LOT BURDENED IS TURFED.

AS PER 88B RESTRICTION NO 10
NO DEVELOPMENT INCLUDING EARTHWORKS, BUILDINGS, FOOTINGS/FOUNDATIONS AND ASSOCIATED INFRASTRUCTURE SHALL BE CARRIED OUT OR CONSTRUCTED ON THE LOTS HEREBY BURDENED UNLESS HAVE BEEN DESIGNED BY A QUALIFIED CIVIL/STRUCTURAL ENGINEER BASED ON GEO-TECHNICAL ADVICE FROM A QUALIFIED GEOTECHNICAL CONSULTANT.

AS PER 88B RESTRICTION NO 12
NO DEVELOPMENT WORKS INCLUDING EARTHWORKS, IMPORTED FILL, LANDSCAPING, ROADS, BUILDINGS, AND ASSOCIATED INFRASTRUCTURE SHALL BE CARRIED OUT OR CONSTRUCTED ON THE LOTS HEREBY BURDENED UNLESS IN ACCORDANCE WITH THE THE MANAGEMENT STRATEGIES AS CONTAINED WITHIN THE REPORT TITLED - POST-CONSTRUCTION SALINITY

WATERPROOFING TO ALL WET AREAS NEEDS TO BE EITHER COMPLY WITH PART 10.2 OF THE ABCB HOUSING PROVISIONS STANDARD 2022 (BCA) OR AS 3740.2021 & 10.2.1 TO 10.2.6 AND 10.2.12 OF THE ABCB HOUSING PROVISIONS STANDARD 2022.

WET AREAS: FALL TO FLOOR WASTE TO BE MINIMUM 1:80 TO MAXIMUM 1:50.

GENERAL NOTES:
•BUILDER TO PROVIDE SLAB UNDER RWT, AC OUTDOOR UNIT & BINS AREA
•BUILDER TO PROVIDE PROVISION FOR DISHWASHER, LAUNDRY MACHINE, DRYER, FRIDGE & TV
•BUILDER TO PROVIDE PROVISION OF WATER CONNECTION IN FRIDGE SPACE •KITCHEN RANGEHOOD DUCTED TO FACADE AND TO COMPLY WITH REQUIREMNTS OF NCC
•ALL ROBES IN THE BEDROOM 600mm DEEP, UNLESS OTHERWISE NOTED
•STAIR RISERS, TREADS & BALUSTRADES TO COMPLY WITH REQUIREMNTS OF NCC •ALL STAIRS STRUCTURE TO STRUCTURAL ENGINEERS DETAILS AND AS PER NCC PART 11.2
•BALUSTRADES AS REQUIRED TO STRUCTURAL ENG'S DETAILS & NCC REQUIREMENTS

•LOCATIONS OF MECH. VENTS, SMOKE ALARMS & FLOOR WASTE SHOWN ON PLANS IS INDICATIVE ONLY. BUILDER TO CORDINATE ON SITE AND COMPLY WITH NCC & RELEVANT AUS. STANDARDS
•SMOKE ALARM IN ACCORDANCE WITH NCC PART 9.5.2, 9.5.4 & AS3786 •SMOKE ALARM POWDERED FROM CONSUMER MAINS SOURCE AND INTERCONNECTED •ALL WET AREAS TO COMPLY WITH NCC PART 10.2 & AS3740
•EXHAUST FROM ALL BATHROOMS/SANITARY COMPARTMENT, KITCHEN & LAUNDRY TO COMPLY WITH NCC PART 10.8. THEY NEED TO DISCHARGE DIRECTLY TO OUTDOOR AIR/EXTERNALLY DUCTED.
•THIS EXHAUST SYSTEM MUST BE INTERLOCKED WITH ROOM'S LIGHT SWITCH AND INCLUDE A RUN-ON TIMER SO THAT THE EXHAUST SYSTEM CONTINUES TO OPERATE FOR 10 MINUTES AFTER THE LIGHT SWITCH IS OFF.

WALL TYPES:
EXTERNAL WALLS: BRICK (110mm) + INSULATION TO BASIX + ONE LAYER OF 10MM STANDARD PLASTERBOARD SCREW FIXED TO TIMBER FRAME SPACED AS PER MANUFACTURE DETAIL INTERNAL WALLS: 10MM PLASTERBOARD SCREW FIXED TO TIMBER STUD FRAME

STONEGROVE HOMES

Rev	Description	Date	App'd
-	CDC DRAWING ISSUED FOR APPROVAL	06.08.26	

Project
PROPOSED DOUBLE STOREY RESIDENCE

7 CATALANA STREET, SPRING FARM 2570
LOT 43, DP1316318

HIRA DESIGNS
Business Address: 13 Feathertop Ave, MINTO NSW 2566
Postal Address: 13 Feathertop Ave, MINTO NSW 2566
Phone Number: 0415112594
Email: info@hiradesigns.com.au
Project Designer:
Pramila Maharjan

Drawing Title
CDC DRAWINGS
FIRST FLOOR PLAN

Checked/Approved
PM

Scale
1:100 @A3 Sheet Size

Project Number
475041


Drawing Number Revision
CDC-104 -

Status
CDC DRAWINGS

HIRA DESIGNS ©
This drawing remains the property of Hira Designs. It may be used for the purpose for which it was commissioned & in accordance with the terms of engagement for that commission.

Copyright HIRA DESIGNS ©


Notes
1. CONTRACTOR MUST VERIFY ALL DIMENSIONS ON SITE BEFORE COMMENCING WORK OR PREPARING SHOP DRAWINGS.
2. DO NOT SCALE DRAWINGS.
3. CONTRACTOR TO CHECK UNDERGROUND SERVICES BEFORE COMMENCING WORKS BY CONTACTING DIAL BEFORE YOU DIG. IF DIAL BEFORE YOU DIG INFORMATION IS PROVIDED WITH THIS DOCUMENTATION IT SHALL BE ASSUMED NOT TO BE CURRENT AND CONTRACTOR SHALL MAKE THEIR OWN ENQUIRES.

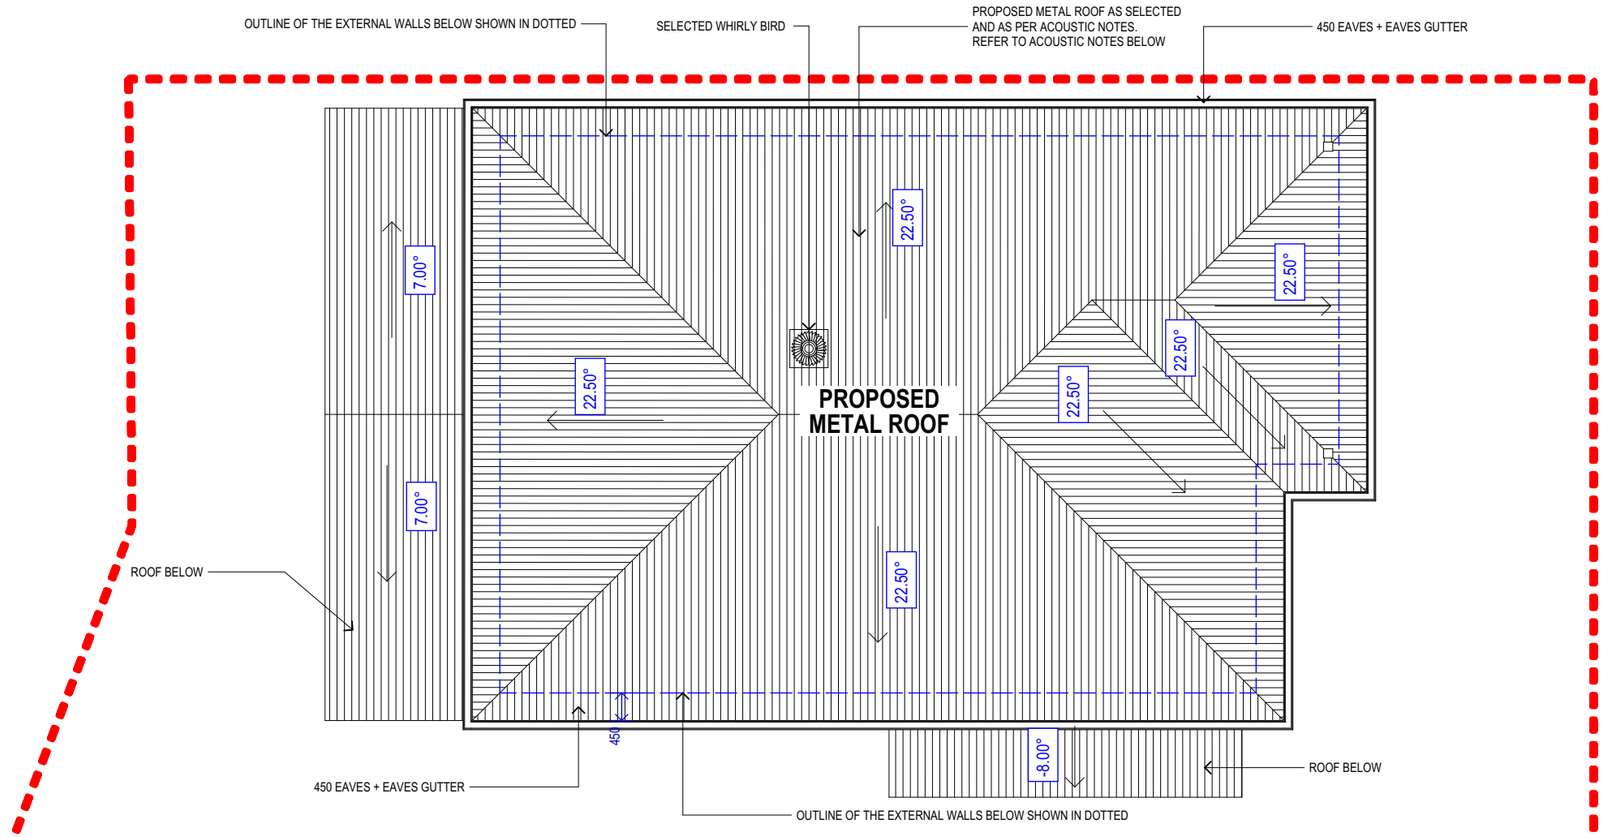

ROOF 1:100

MIN. PITCH REQUIREMENTS FOR METAL ROOFING PROFILES TO NCC PART 7.2

Figure 7.2.3 Minimum pitch requirements for metal roofing profiles

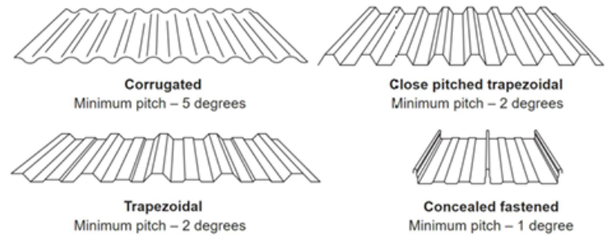

ROOF PLAN TO BE READ IN CONJUCTION WITH THE STROMWATER DESIGN, DRAWINGS AND DETAILS

VENTILATION OF ROOF SPACES TO COMPLY WITH NCC REQUIREMENTS (HP PART 10.8.3)

NOTES:
- ALL ROOF CLADDING IS TO BE IN ACCORDANCE WITH AS.1562.1
- ALL GUTTERS & DOWNPIPES TO COMPLY WITH NCC PART 7.4 AND AS/NZS 3500.3: 2021
- ALL ROOF AND WALL CLADDING TO BE DESIGNED AND INSTALLED IN ACCORDANCE WITH NCC 2022 H1D7
- ROOFSHEETING, CAPPING, GUTTERS, FASCIA & DOWNPIPES TO BE INSTALLED TO MANUFACTURERS SPECIFICATIONS AND REQUIREMENTS.
- ALL DOWN PIPES TO JOIN COUNCIL'S STORM WATER SYSTEM.
- ALL DOWNPIPES TO BE PVC, CIRCULAR & PLUMBER TO CONNECT THE DP'STO GUTTER.
- LOCATION OF DOWN PIPES IS INDICATIVE ONLY,TO BE COORDINATED ON SITE BY THE PLUMBER.

Sydney Wide Certifiers Pty Ltd
Complying Development Certificate
Reference: SWC262403/01
Date: 13/10/2026
Sandres Markhani BDC05035

AS PER 88B RESTRICTION NO 7
4.NO BUILDING OR BUILDINGS SHALL BE ERECTED OR BE PERMITTED TO REMAIN ERECTED ON ANY LOT BURDENED OTHER THAN WITH EXTERNAL WALLS OF BRICK AND/OR BRICK VENEER AND/OR STONE AND/OR CONCRETE AND/OR GLASS AND/OR TIMBER AND/OR HARDIPLANK OR SIMILAR PRODUCT. NO BUILDING OR BUILDINGS SHALL BE ERECTED OR PERMITTED TO REMAIN ERECTED ON ANY LOT BURDENED HAVING A ROOF OTHER THAN CLAY TILES, CEMENT TILES, SLATE OR NON REFTECTIVE SURFACE CORRUGATED IRON. ALL ROOFING MATERIALS SHALL BE NEUTRAL COLOURS OR SHADES OF GREY.
6.NO FENCE SHALL BE ERECTED OR PERMITTED TO REMAIN ON ANY LOT HEREBY BURDENED UNLESS THE FENCING IS OF A TIMBER LAPPED AND/OR LAPPED AND CAPPED CONSTRUCTION OR COLORBOND FENCE PROVIDED THAT COLORBOND FENCE CAN ONLY USE COLOURS, SHALE GREY, DUNE, BASALT OR WOODLAND GREY.
8.NO ADVERTISING HOARDING SIGNS OR MATTER SHALL BE DISPLAYED OR ERECTED ON ANY LOT BURDENED (OTHER THAN A SIGN ADVERTISING THAT THE SAID LOT IS FOR SALE) WITHOUT THE PRIOR WRITTEN CONSENT OF MACARTHUR 215 PTY LIMITED OR ITS SUCCESSORS IN TITLE OR ASSIGNS.
9.NO DRIVEWAY SHALL BE CONSTRUCTED ON ANY LOT BURDENED UNLESS ITS SURFACE IS COMPRISED OF FAUX, STAMPED OR COLOURED CONCRETE OR PAVERS OR AS APPROVED BY MACARTHUR 215 PTY LIMITED OR ITS ASSIGNS AND UNLESS DRIVEWAY CONSTRUCTION IS UNDERTAKEN PRIOR TO PRACTICAL COMPLETION OF THE MAIN BUILDING.
10.NO DWELLING SHALL BE ERECTED OR PERMITTED TO REMAIN ON ANY LOT BURDENED UNLESS THE AREA BETWEEN THE BUILDING LINE AND THE FRONT BOUNDARY OF THE LOT BURDENED IS TURFED.

AS PER 88B RESTRICTION NO 10
NO DEVELOPMENT INCLUDING EARTHWORKS, BUILDINGS, FOOTINGS/FOUNDATIONS AND ASSOCIATED INFRASTRUCTURE SHALL BE CARRIED OUT OR CONSTRUCTED ON THE LOTS HEREBY BURDENED UNLESS HAVE BEEN DESIGNED BY A QUALIFIED CIVIL/STRUCTURAL ENGINEER BASED ON GEO-TECHNICAL ADVICE FROM A QUALIFIED GEOTECHNICAL CONSULTANT.

AS PER 88B RESTRICTION NO 12
NO DEVELOPMENT WORKS INCLUDING EARTHWORKS, IMPORTED FILL, LANDSCAPING, ROADS, BUILDINGS, AND ASSOCIATED INFRASTRUCTURE SHALL BE CARRIED OUT OR CONSTRUCTED ON THE LOTS HEREBY BURDENED UNLESS IN ACCORDANCE WITH THE MANAGEMENT STRATEGIES AS CONTAINED WITHIN THE REPORT TITLED - POST-CONSTRUCTION SALINITY

HIRA DESIGNS ©
This drawing remains the property of Hira Designs. It may be used for the purpose for which it was commissioned & in accordance with the terms of engagement for that commission.

Rev	Description	Date	App'd
-	CDC DRAWING ISSUED FOR APPROVAL	06.08.26	

Project
PROPOSED DOUBLE STOREY RESIDENCE

7 CATALANA STREET, SPRING FARM 2570
LOT 43, DP1316318

HIRA DESIGNS
Business Address: 13 Feathertop Ave, MINTO NSW 2566
Postal Address: 13 Feathertop Ave, MINTO NSW 2566
Phone Number: 0415112594
Email: info@hiradesigns.com.au
Project Designer:
Pramila Maharjan

Drawing Title
CDC DRAWINGS
ROOF PLAN

Checked/Approved
PM

Scale
1:100 @A3 Sheet Size

Project Number
475041


Drawing Number Revision
CDC-105 -

Status
CDC DRAWINGS


STONEGROVE HOMES

NOTES: REFER STRUCTURAL ENGINEER'S DRAWINGS & DETAILS FOR THE FOLLOWING;
•CONCRETE SLAB & FOOTINGS, EDGE/DROP BEAM DETAILS AND ALL BRICK REBATES
•EXPANSION JOINTS (WHERE REQUIRED) TO BE PROVIDED AS PER NCC/AUSTRALIAN STANDARDS.
FLOOR FINISH LEVEL NEEDS TO BE 150MM ABOVE THE NATURAL GROUND LEVEL.
BUILDING ELEVATIONS TO BE READ IN CONJUNCTION WITH FINISHES SCHEDULE

•TIMBER & SHEET WALL CLADDING TO COMPLY WITH NCC PART 7.5.2, 7.5.4 & 7.5.7
•EAVES & SOFFIT LININGS TO COMPLY WITH NCC PART 7.5.5
•PARAPET CAPPINGS TO COMPLY WITH NCC PART 7.5.8

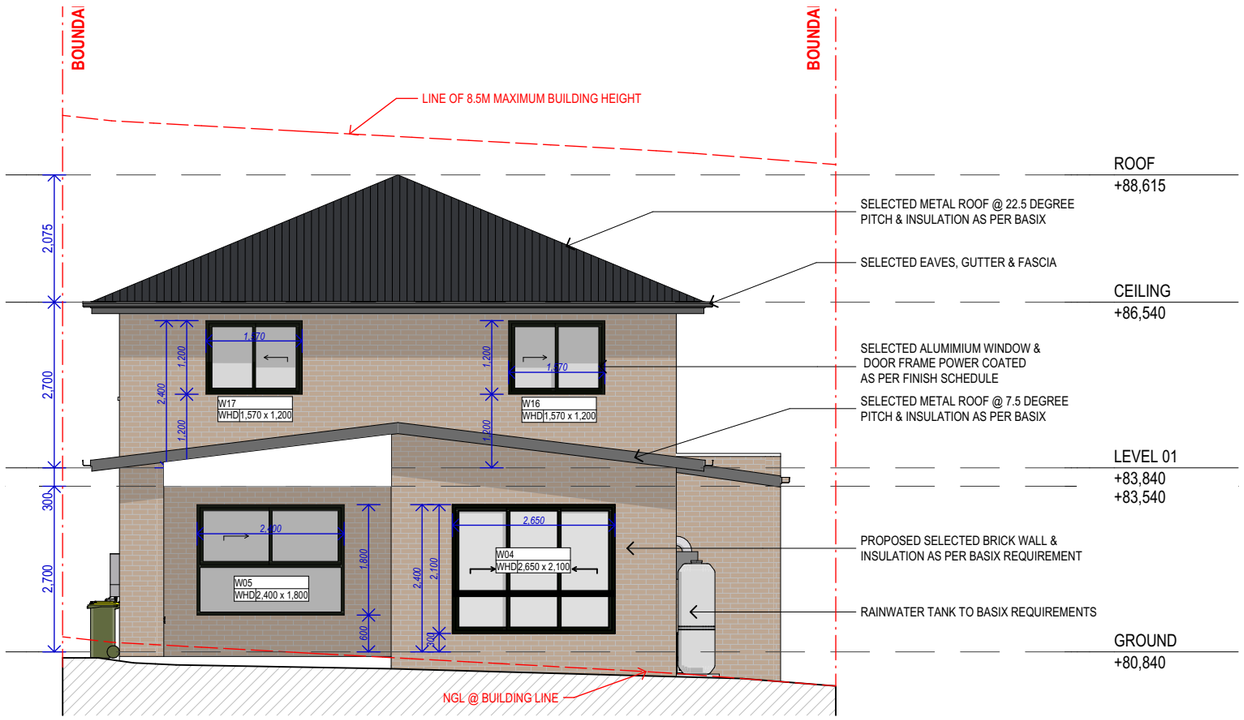

WEST ELEVATION 1:100

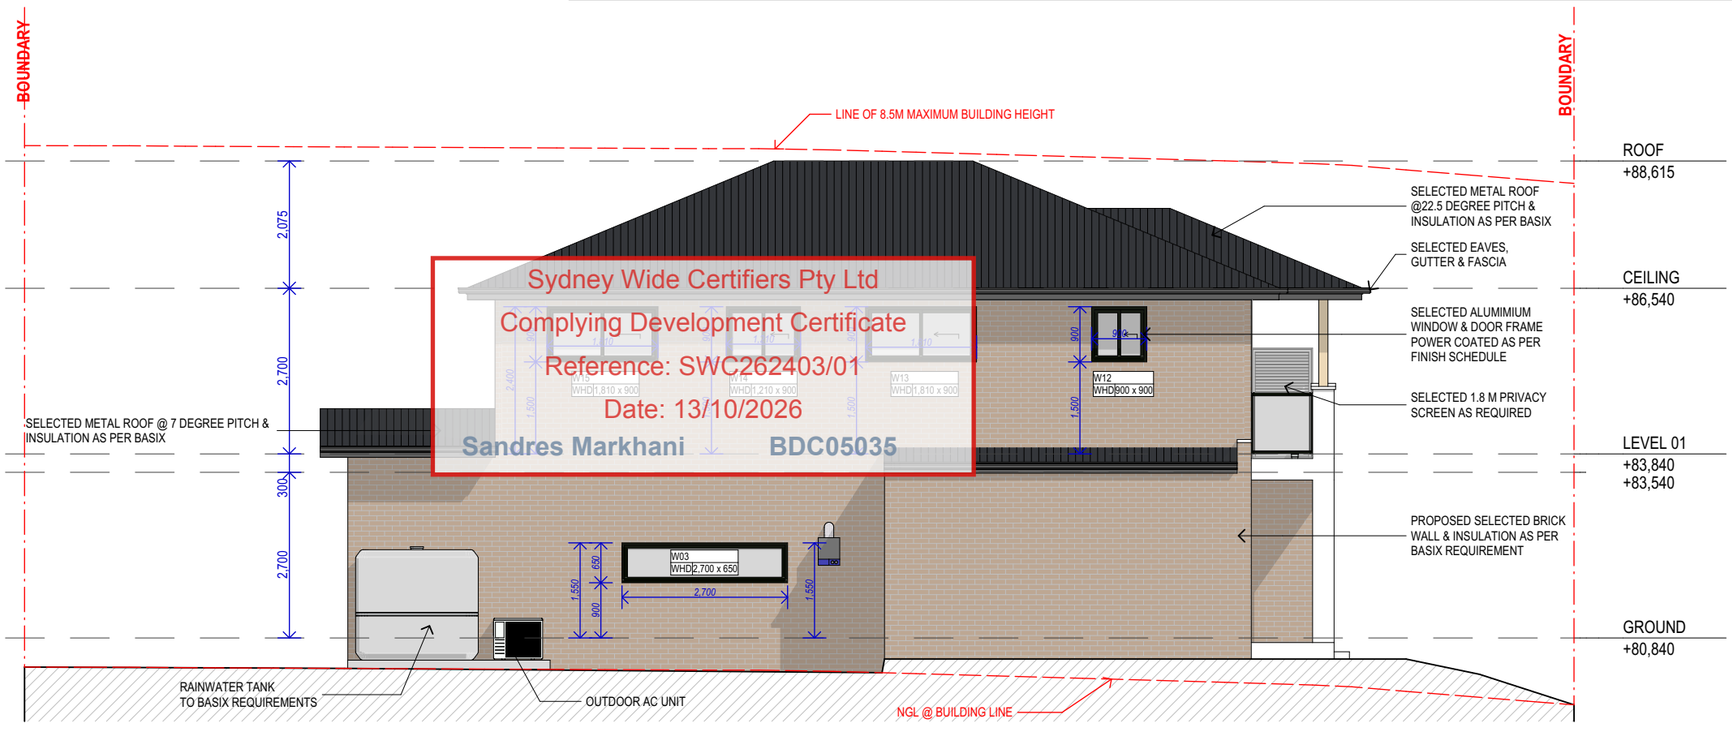

SOUTH ELEVATION 1:100

Sydney Wide Certifiers Pty Ltd
Complying Development Certificate
Reference: SWC262403/01
Date: 13/10/2026
Sandres Markhani BDC05035

Copyright HIRA DESIGNS ©

Notes
1. CONTRACTOR MUST VERIFY ALL DIMENSIONS ON SITE BEFORE COMMENCING WORK OR PREPARING SHOP DRAWINGS.
2. DO NOT SCALE DRAWINGS.
3. CONTRACTOR TO CHECK UNDERGROUND SERVICES BEFORE COMMENCING WORKS BY CONTACTING DIAL BEFORE YOU DIG. IF DIAL BEFORE YOU DIG INFORMATION IS PROVIDED WITH THIS DOCUMENTATION IT SHALL BE ASSUMED NOT TO BE CURRENT AND CONTRACTOR SHALL MAKE THEIR OWN ENQUIRES.

Rev	Description	Date	App'd
-	CDC DRAWING ISSUED FOR APPROVAL	06.08.26	

Project
PROPOSED DOUBLE STOREY RESIDENCE
7 CATALANA STREET, SPRING FARM 2570
LOT 43, DP1316318

HIRA DESIGNS
Business Address: 13 Feathertop Ave, MINTO NSW 2566
Postal Address: 13 Feathertop Ave, MINTO NSW 2566
Phone Number: 0415112594
Email: info@hiradesigns.com.au
Project Designer:
Pramila Maharjan

Drawing Title
CDC DRAWINGS
WEST/SOUTH ELEVATIONS

Checked/Approved
PM

Scale
1:100 @A3 Sheet Size

Project Number
475041

Drawing Number Revision
CDC-106 -

Status
CDC DRAWINGS

STONEGROVE HOMES


erty of Hira Designs. It may be used for the purpose for which it
dance with the terms of engagement for that commission.

NOTES: REFER STRUCTURAL ENGINEER'S DRAWINGS & DETAILS FOR THE FOLLOWING;
•CONCRETE SLAB & FOOTINGS, EDGE/DROP BEAM DETAILS AND ALL BRICK REBATES
•EXPANSION JOINTS (WHERE REQUIRED) TO BE PROVIDED AS PER NCC/AUSTRALIAN STANDARDS.
FLOOR FINISH LEVEL NEEDS TO BE 150MM ABOVE THE NATURAL GROUND LEVEL.
BUILDING ELEVATIONS TO BE READ IN CONJUNCTION WITH FINISHES SCHEDULE


•TIMBER & SHEET WALL CLADDING TO COMPLY WITH NCC PART 7.5.2, 7.5.4 & 7.5.7
•EAVES & SOFFIT LININGS TO COMPLY WITH NCC PART 7.5.5
•PARAPET CAPPINGS TO COMPLY WITH NCC PART 7.5.8

Copyright HIRA DESIGNS ©

Notes
1. CONTRACTOR MUST VERIFY ALL DIMENSIONS ON SITE BEFORE COMMENCING WORK OR PREPARING SHOP DRAWINGS.
2. DO NOT SCALE DRAWINGS.
3. CONTRACTOR TO CHECK UNDERGROUND SERVICES BEFORE COMMENCING WORKS BY CONTACTING DIAL BEFORE YOU DIG. IF DIAL BEFORE YOU DIG INFORMATION IS PROVIDED WITH THIS DOCUMENTATION IT SHALL BE ASSUMED NOT TO BE CURRENT AND CONTRACTOR SHALL MAKE THEIR OWN ENQUIRES.

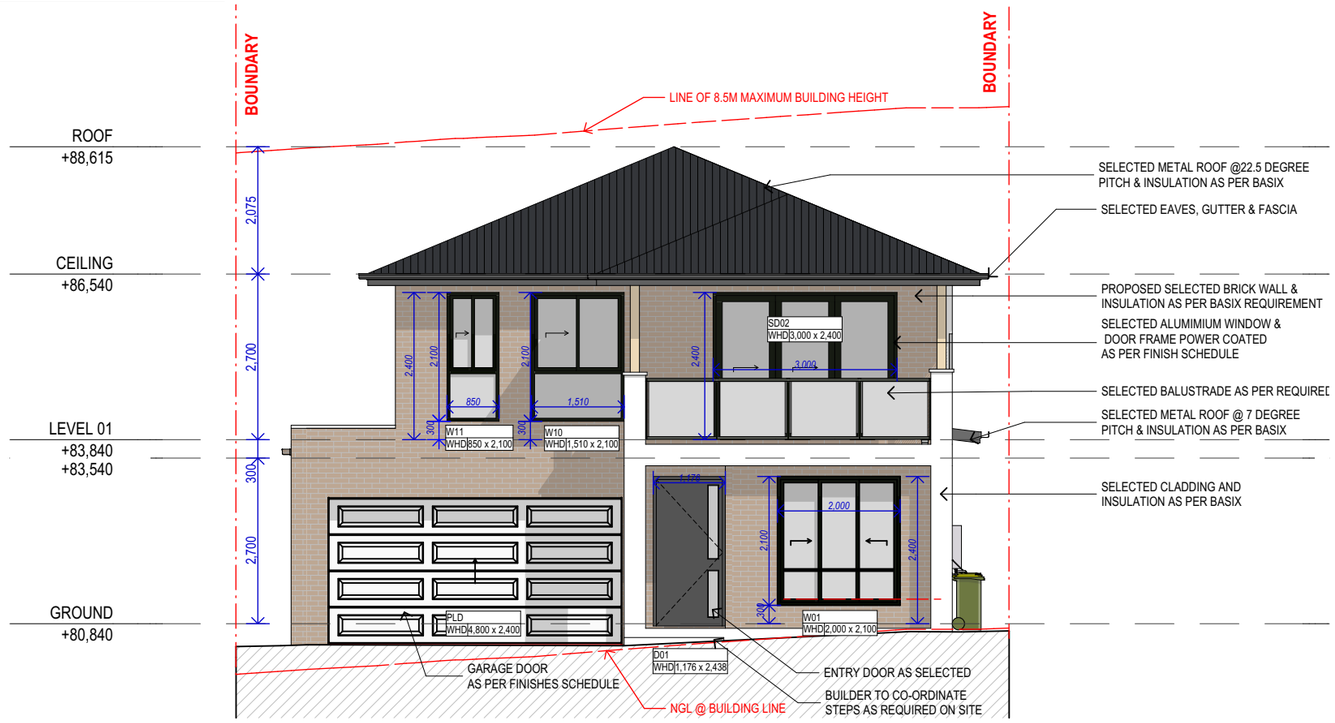

EAST ELEVATION 1:100

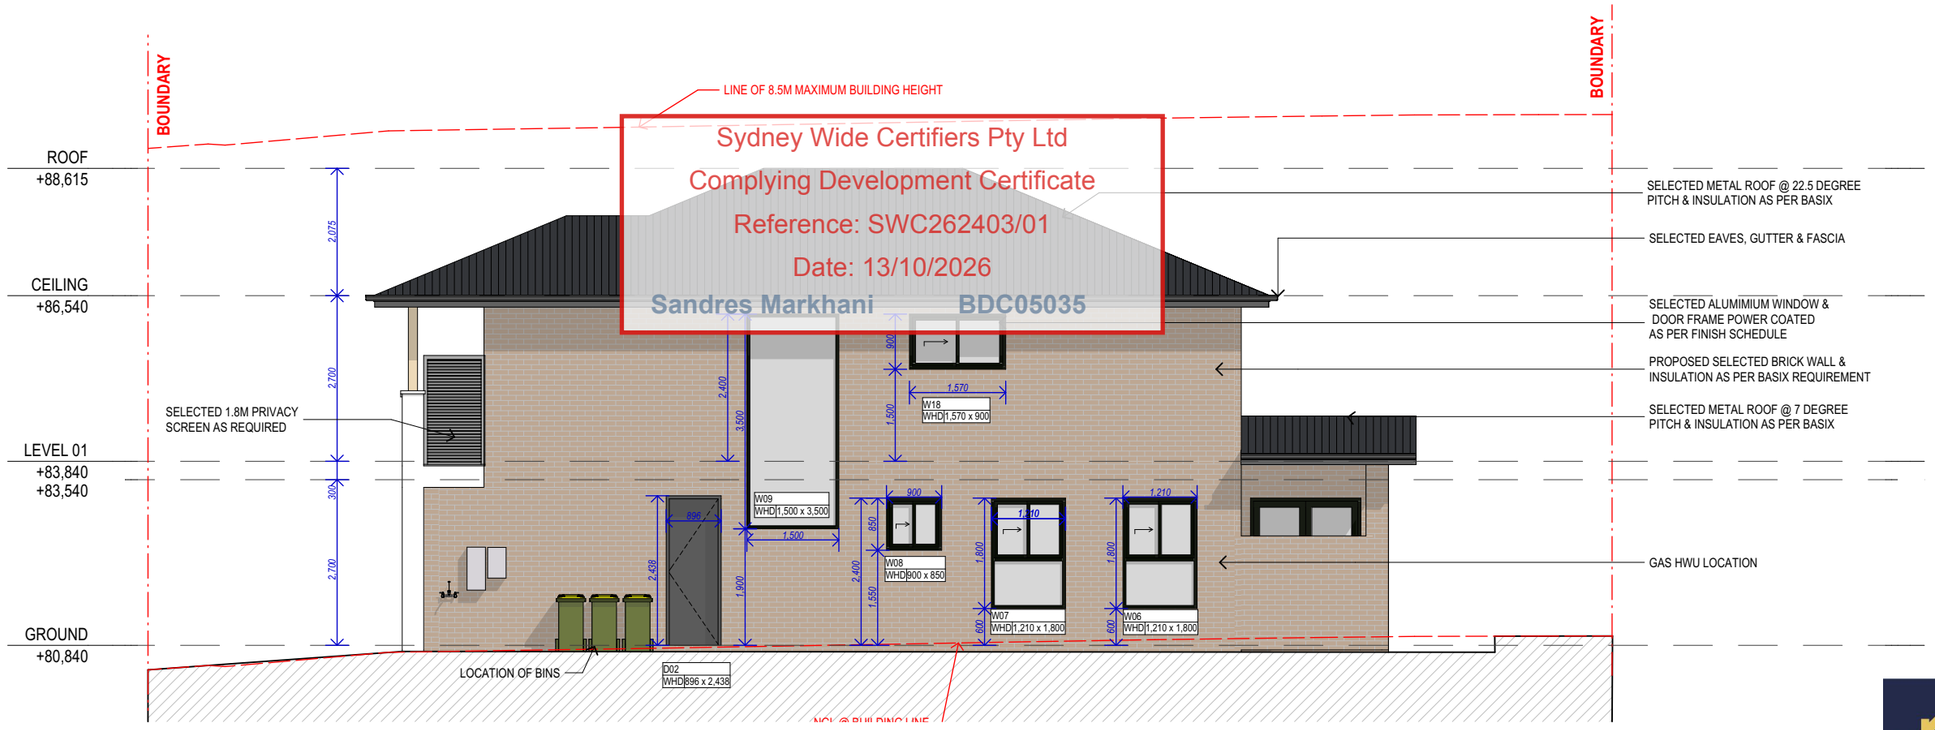

NORTH ELEVATION 1:100

erty of Hira Designs. It may be used for the purpose for which it
dance with the terms of engagement for that commission.

Rev	Description	Date	App'd
-	CDC DRAWING ISSUED FOR APPROVAL	06.08.26	

Project
PROPOSED DOUBLE STOREY RESIDENCE

7 CATALANA STREET, SPRING FARM 2570
LOT 43, DP1316318

HIRA DESIGNS
Business Address: 13 Feathertop Ave, MINTO NSW 2566
Postal Address: 13 Feathertop Ave, MINTO NSW 2566
Phone Number: 0415112594
Email: info@hiradesigns.com.au
Project Designer:
Pramila Maharjan

Drawing Title
CDC DRAWINGS
EAST/NORTH ELEVATIONS

Checked/Approved
PM

Scale
1:100 @A3 Sheet Size

Project Number
475041

Drawing Number Revision
CDC-107 -

Status
CDC DRAWINGS


STONEGROVE HOMES

NOTES: REFER STRUCTURAL ENGINEER'S DRAWINGS & DETAILS FOR THE FOLLOWING;
•CONCRETE SLAB & FOOTINGS, EDGE/DROP BEAM DETAILS AND ALL BRICK REBATES
•EXPANSION JOINTS (WHERE REQUIRED) TO BE PROVIDED AS PER NCC/AUSTRALIAN STANDARDS.
FLOOR FINISH LEVEL NEEDS TO BE 150MM ABOVE THE NATURAL GROUND LEVEL.
BUILDING ELEVATIONS TO BE READ IN CONJUNCTION WITH FINISHES SCHEDULE


•TIMBER & SHEET WALL CLADDING TO COMPLY WITH NCC PART 7.5.2, 7.5.4 & 7.5.7
•EAVES & SOFFIT LININGS TO COMPLY WITH NCC PART 7.5.5
•PARAPET CAPPINGS TO COMPLY WITH NCC PART 7.5.8

Copyright HIRA DESIGNS ©

Notes
1. CONTRACTOR MUST VERIFY ALL DIMENSIONS ON SITE BEFORE COMMENCING WORK OR PREPARING SHOP DRAWINGS.
2. DO NOT SCALE DRAWINGS.
3. CONTRACTOR TO CHECK UNDERGROUND SERVICES BEFORE COMMENCING WORKS BY CONTACTING DIAL BEFORE YOU DIG. IF DIAL BEFORE YOU DIG INFORMATION IS PROVIDED WITH THIS DOCUMENTATION IT SHALL BE ASSUMED NOT TO BE CURRENT AND CONTRACTOR SHALL MAKE THEIR OWN ENQUIRES.

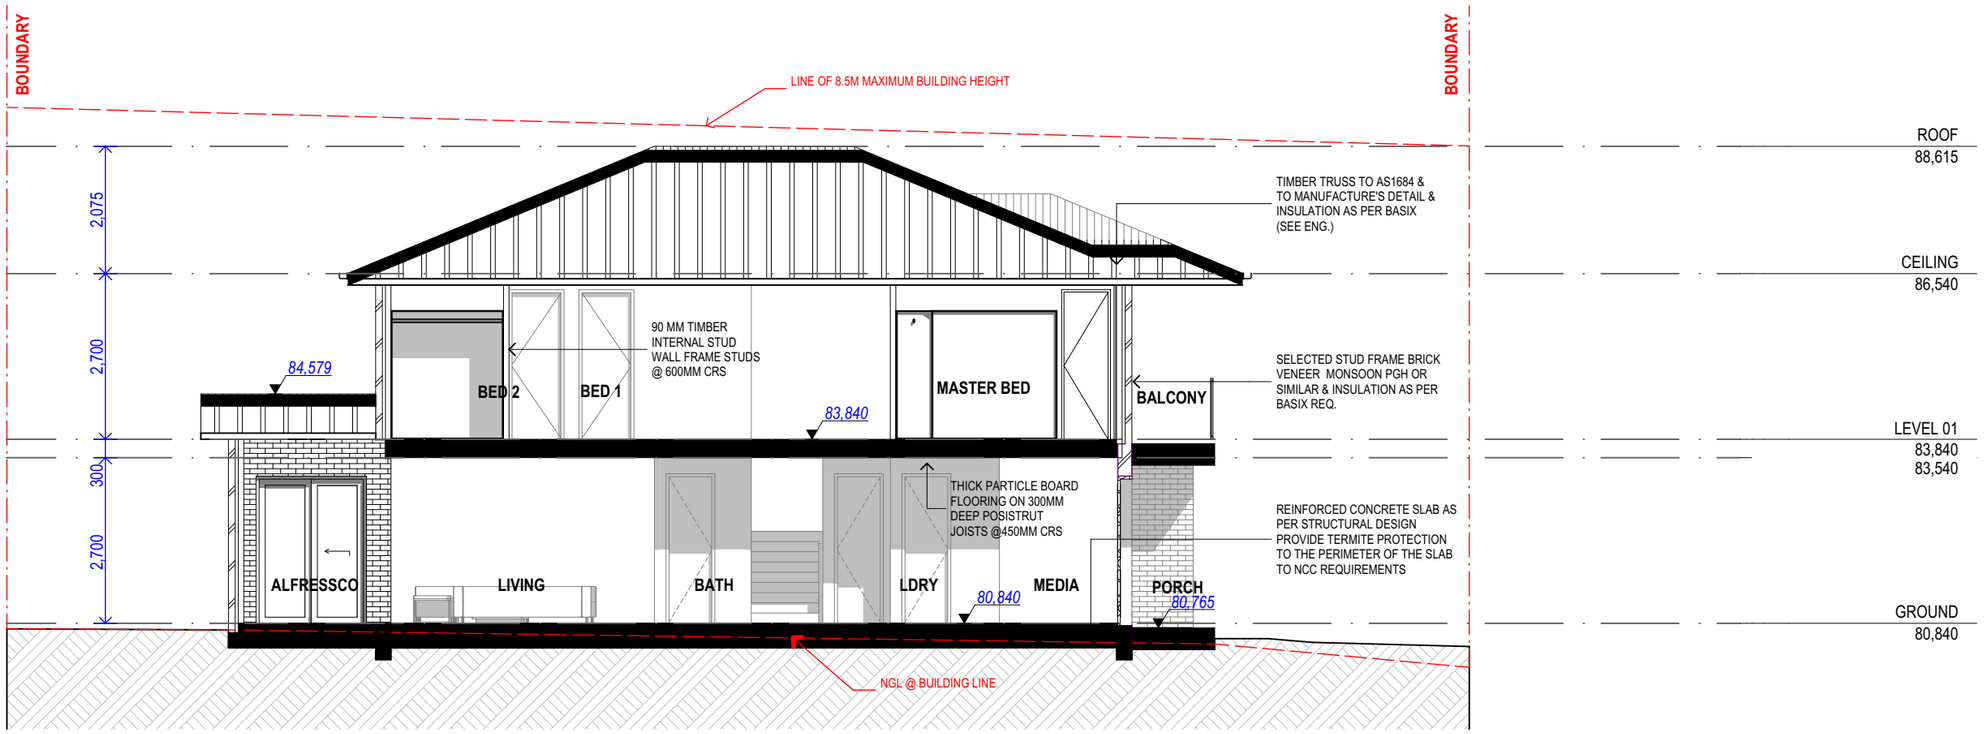

SECTION AT AA 1:100

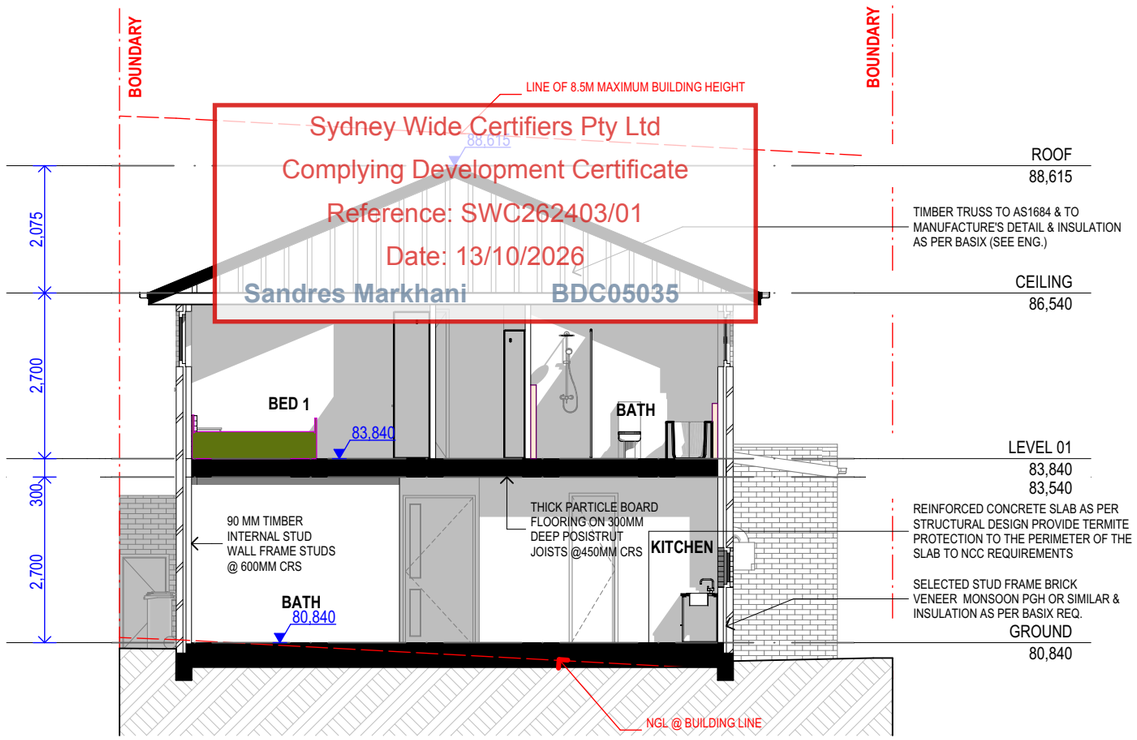

Sydney Wide Certifiers Pty Ltd
Complying Development Certificate
Reference: SWC262403/01
Date: 13/10/2026
Sandres Markhani BDC05035

SECTION AT BB 1:100

HIRA DESIGNS ©
This drawing remains the property of Hira Designs. It may be used for the purpose for which it was commissioned & in accordance with the terms of engagement for that commission.

Rev	Description	Date	App'd
-	CDC DRAWING ISSUED FOR APPROVAL	06.08.26	

Project
PROPOSED DOUBLE STOREY RESIDENCE

7 CATALANA STREET, SPRING FARM 2570
LOT 43, DP1316318

HIRA DESIGNS
Business Address: 13 Feathertop Ave, MINTO NSW 2566
Postal Address: 13 Feathertop Ave, MINTO NSW 2566
Phone Number: 0415112594
Email: info@hiradesigns.com.au
Project Designer:
Pramila Maharjan

Drawing Title
CDC DRAWINGS
SECTION

Checked/Approved
PM

Scale
1:100 @A3 Sheet Size

Project Number
475041








Drawing Number Revision
CDC-108 -

Status
CDC DRAWINGS








STONEGROVE HOMES

Copyright HIRA DESIGNS ©

Notes
1. CONTRACTOR MUST VERIFY ALL DIMENSIONS ON SITE BEFORE COMMENCING WORK OR PREPARING SHOP DRAWINGS.
2. DO NOT SCALE DRAWINGS.
3. CONTRACTOR TO CHECK UNDERGROUND SERVICES BEFORE COMMENCING WORKS BY CONTACTING DIAL BEFORE YOU DIG. IF DIAL BEFORE YOU DIG INFORMATION IS PROVIDED WITH THIS DOCUMENTATION IT SHALL BE ASSUMED NOT TO BE CURRENT AND CONTRACTOR SHALL MAKE THEIR OWN ENQUIRES.

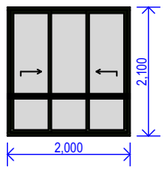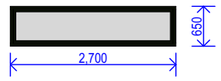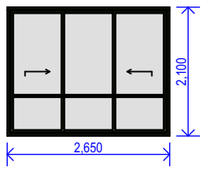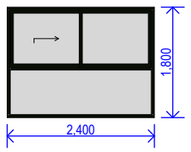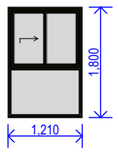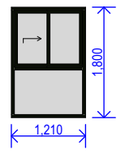
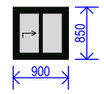
GROUND FLOOR WINDOW SCHEDULE							
ID	W01	W03	W04	W05	W06	W07	W08
HEIGHT	2,100	650	2,100	1,800	1,800	1,800	850
WIDTH	2,000	2,700	2,650	2,400	1,210	1,210	900
Elevation							

GROUND FLOOR WINDOW SCHEDULE 1:1

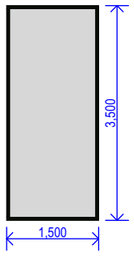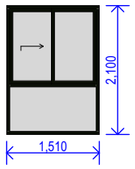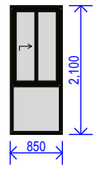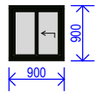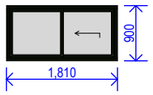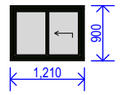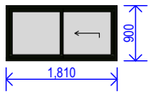FIRST FLOOR WINDOW SCHEDULE							
ID	W09	W10	W11	W12	W13	W14	W15
HEIGHT	3,500	2,100	2,100	900	900	900	900
WIDTH	1,500	1,510	850	900	1,810	1,210	1,810
Elevation							

FIRST FLOOR WINDOW SCHEDULE 1:1

Sydney Wide Certifiers Pty Ltd
Complying Development Certificate
Reference: SWC262403/01
Date: 13/10/2026
Sandres Markhani BDC05035

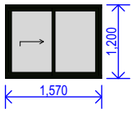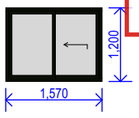FIRST FLOOR WINDOW SCHEDULE							
ID	W16		W17				
HEIGHT	1,200		1,200				
WIDTH	1,570		1,570				
Elevation							

FIRST FLOOR WINDOW SCHEDULE 1:1

HIRA DESIGNS ©
This drawing remains the property of Hira Designs. It may be used for the purpose for which it was commissioned & in accordance with the terms of engagement for that commission.

Rev	Description	Date	App'd
-	CDC DRAWING ISSUED FOR APPROVAL	06.08.26	

Project
PROPOSED DOUBLE STOREY RESIDENCE

7 CATALANA STREET, SPRING FARM 2570
LOT 43, DP1316318

HIRA DESIGNS
Business Address: 13 Feathertop Ave, MINTO NSW 2566
Postal Address: 13 Feathertop Ave, MINTO NSW 2566
Phone Number: 0415112594
Email: info@hiradesigns.com.au
Project Designer:
Pramila Maharjan

Drawing Title
CDC DRAWINGS
WINDOW SCHEDULE

Checked/Approved
PM

Scale
1:1 @A3 Sheet Size

Project Number
475041




Drawing Number Revision
CDC-111 -

Status
CDC DRAWINGS

STONEGROVE HOMES

Copyright HIRA DESIGNS ©

Notes
1. CONTRACTOR MUST VERIFY ALL DIMENSIONS ON SITE BEFORE COMMENCING WORK OR PREPARING SHOP DRAWINGS.
2. DO NOT SCALE DRAWINGS.
3. CONTRACTOR TO CHECK UNDERGROUND SERVICES BEFORE COMMENCING WORKS BY CONTACTING DIAL BEFORE YOU DIG. IF DIAL BEFORE YOU DIG INFORMATION IS PROVIDED WITH THIS DOCUMENTATION IT SHALL BE ASSUMED NOT TO BE CURRENT AND CONTRACTOR SHALL MAKE THEIR OWN ENQUIRES.

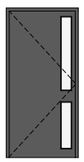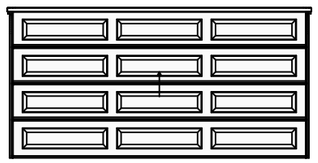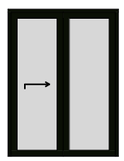GROUND FLOOR DOOR SCHEDULE					
ID	D01	D02	D03	PLD	SD01
QUNATITY	1	2	4	1	1
HEIGHT	2,400	2,400	2,400	2,400	2,400
WIDTH	1,100	820	720	4,800	1,800
COMMENTS	ENTRY DOOR	SOLID HINGE DOOR	SOLID HINGE DOOR	PANEL LIFT DOOR	SLIDING DOOR
ELEVATION					

GROUND FLOOR DOOR SCHEDULE 1:1

FIRST FLOOR DOOR SCHEDULE			
ID	D04	D05	SD02
QUNATITY	4	3	1
HEIGHT	2,400	2,400	2,400
WIDTH	820	720	3,000
COMMENTS	SOLID HINGE DOOR	SOLID HINGE DOOR	SLIDING DOOR
ELEVATION			

FIRST FLOOR DOOR SCHEDULE 1:1

Sydney Wide Certifiers Pty Ltd
Complying Development Certificate
Reference: SWC262403/01
Date: 13/10/2026
Sandres Markhani BDC05035

HIRA DESIGNS ©
This drawing remains the property of Hira Designs. It may be used for the purpose for which it was commissioned & in accordance with the terms of engagement for that commission.

Rev	Description	Date	App'd
-	CDC DRAWING ISSUED FOR APPROVAL	06.08.26	

Project
PROPOSED DOUBLE STOREY RESIDENCE
7 CATALANA STREET, SPRING FARM 2570
LOT 43, DP1316318

HIRA DESIGNS
Business Address: 13 Feathertop Ave, MINTO NSW 2566
Postal Address: 13 Feathertop Ave, MINTO NSW 2566
Phone Number: 0415112594
Email: info@hiradesigns.com.au
Project Designer:
Pramila Maharjan

Drawing Title
CDC DRAWINGS
DOOR SCHEDULE

Checked/Approved
PM

Scale
1:1 @A3 Sheet Size

Project Number
475041

Drawing Number Revision
CDC-112 -

Status
CDC DRAWINGS


STONEGROVE HOMES

Copyright HIRA DESIGNS ©

Notes
1. CONTRACTOR MUST VERIFY ALL DIMENSIONS ON SITE BEFORE COMMENCING WORK OR PREPARING SHOP DRAWINGS.
2. DO NOT SCALE DRAWINGS.
3. CONTRACTOR TO CHECK UNDERGROUND SERVICES BEFORE COMMENCING WORKS BY CONTACTING DIAL BEFORE YOU DIG. IF DIAL BEFORE YOU DIG INFORMATION IS PROVIDED WITH THIS DOCUMENTATION IT SHALL BE ASSUMED NOT TO BE CURRENT AND CONTRACTOR SHALL MAKE THEIR OWN ENQUIRES.

LEGEND

– – – – –	EXTENT OF SEDIMENT FENCE
— — —	EXTENT OF TEMP FENCE
	MATERIAL STORAGE ZONE
— — — —	DEMOLITION
	EXCAVATION TO TAKE NEW WORK

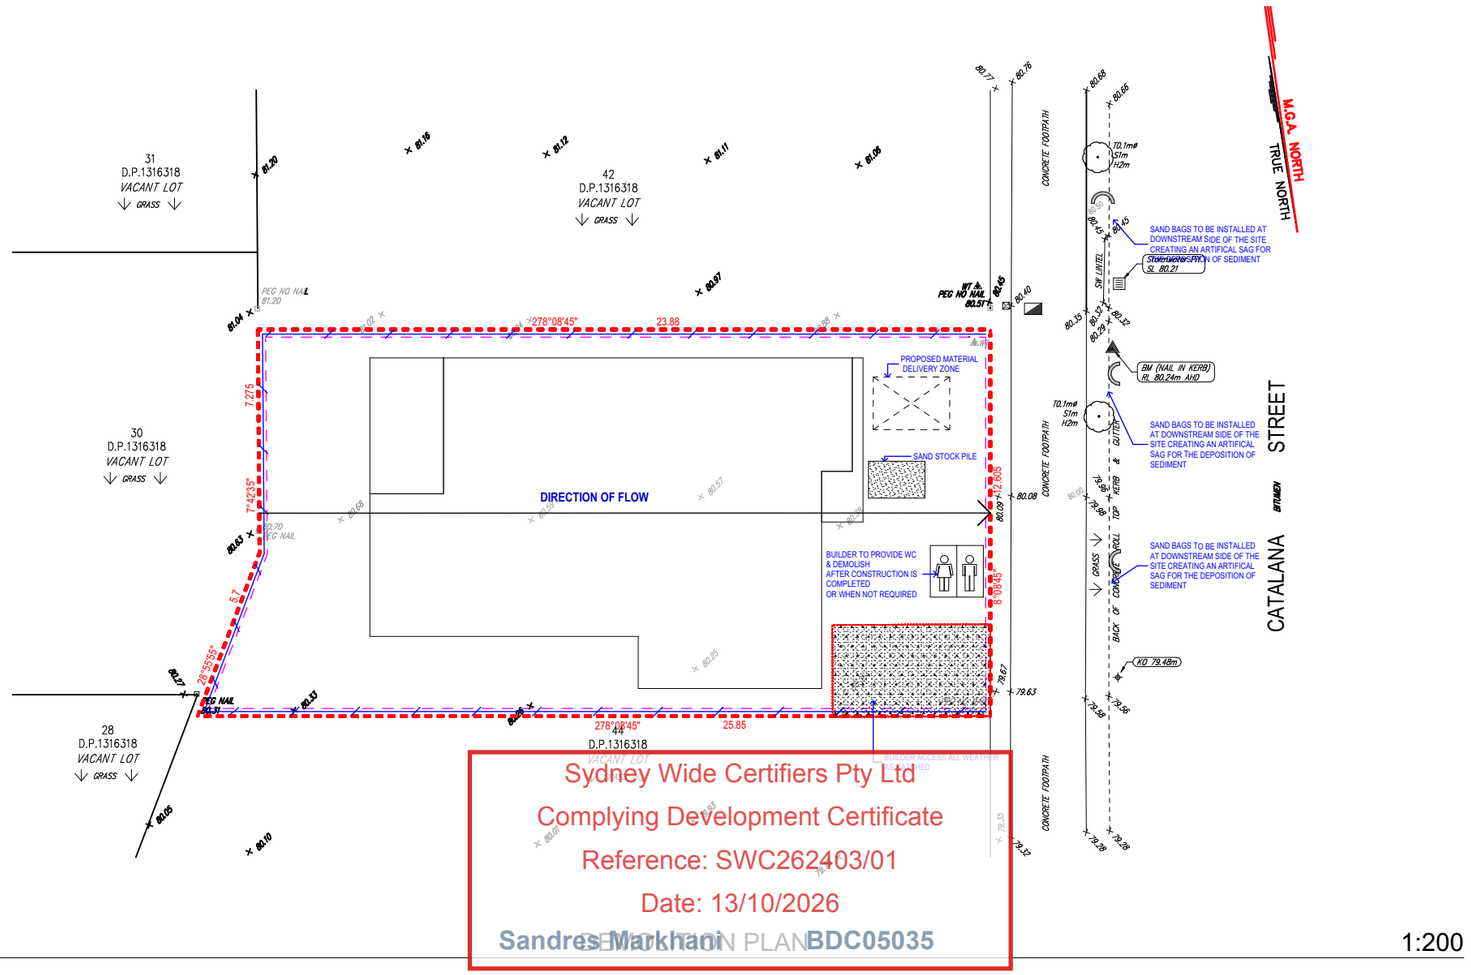

Sydney Wide Certifiers Pty Ltd
Complying Development Certificate
Reference: SWC262403/01
Date: 13/10/2026
Sandres Markhani
SEDIMENTATION PLAN BDC05035


NOTES:

1. FOR EXACTDIMENSION REFER TO SURVEY PLAN


2. CONTRACTOR TO SEAL ALL NON USE SERVICES FOR SAFETY(I.E WATER PIPES/ELECTRICAL LINES/ GAS/TELEPHONE LINES/SEWER CONNECTION ETC. & PROVIDE LOCATION POINTS ON PLAN TO OWNER.
3. ALL SERVICES TO BE CAPPED BY APPROPRIATE & REGISTERED CONTRACTOR AND INSPECTED BY RELEVANT AUTHORITY PERSONNEL

SEDIMENT EROSION CONTROL


1. APPROPRIATE CONTROL MEASURES ARE TO BE UNDERTAKEN FOR CONTROL OF SOIL EROSION AND MINIMISATION OF DOWNSTREAM SEDIMENT TRANSFER DURING THE CONSTRUCTION PERIOD AND FOR FULL PERIOD OF OPERATION OF DEVELOPMENT. THE WORKS SHALL COMPLY WITH THE GENERAL PRINCIPLES AS SET DOWN IN THE PUBLICATION "URBAN CONSERVATION AND SEDIMENT CONTROL" PUBLISHED BY THE SOIL CONSERVATION SERVICE. PARTICULAR ATTENTION SHOULD BE PAID TO SURFACE RUN-OFF FROM ALL EXPOSED AREAS. HAY BAILING TO BE USED WITH STAR PICKETS ANCHORS AT SITE LOW POINTS WHERE APPROPRIATE. ALL EXPOSED SURFACES TO BE TURFED AS REQUIRED ON COMPLETION OF THE SITE WORKS.
3. WINDOW OPENINGS ARE SET AS PER No. OF BRICKS & COURSE HEIGHTS (e.g. 10K-25C) USE NEAREST STANDARD SIZE FROM SELECTED MANUFACTURER.
4. REFER TO ENG. DWG. FOR ALL FOOTINGS, SLABS, RETAINING WALLS, BEAMS, EJS, SOIL COMPACTIONS, PIERS....ETC.
5. ALL SERVICES TO COMPLY WITH B.C.A. & AUST. STANDARDS. CONNECTIONS TO COMPLY WITH APPROPRIATE AUTHORITY REQUIREMENTS AND APPROVALS.
6. CONFIRM ALL LEVELS WITH REGISTERED SURVEYOR PRIOR TO COMMENCEMENT OF WORKS.
7. STORMWATER AND SEWAGE TO BE CONNECTED AND DISCHARGED AS PER AS3500 & ACCE. STD OF DOMESTIC CONST.
8. ALL SERVICES TO BE LOCATED AND VERIFIED BY CONTRACTOR WITH RELEVANT AUTHORITIES PRIOR TO COMMENCEMENT OF ANY BUILDING WORKS. IT IS CLIENT/OWNER'S RESPONSIBILITY TO DO SO PRIOR TO DOCUMENTS PREPARATIONS BY ARCHITECT
9. FOR ANY EXISTING SERVICES & SEWER LOCATION CLIENT/OWNER/CONTRACTOR MUST DO PEGOUT PRIOR OF ANY DOCUMENTATION OR COMMENCEMENT OF CONSTRUCTION
2. CLEAN & PREPARE BLOCK TO TAKE NEW RESIDENCE AS LOCATED ON SITE PLAN. CHECK LEVELS ON SITE. CUT AND FILL AS REQ. CHECK ALL DIMENSIONS.
* TIMBER FRAMING FOR FLOOR, WALL AND ROOF TO MANUFACTURER'S SPECIFICATIONS.
* EXPANSION JOINTS ARE TO BE PROVIDED LEVEL 12 METRES FOR CLAY BRICKS AND LEVEL 6 METERS FOR CONCRETE BRICKS AND IN ACCORDANCE WITH ENGINEER'S SPECIFICATIONS.
* ALL GLAZING TO AUSTRALIAN STANDARD 1208-1994.
* REFER STANDARDS.
* WINDOW SASH LOCATION AND GLAZING BAR CONFIGURATION TO MANUFACTURER'S SPECIFICATIONS.

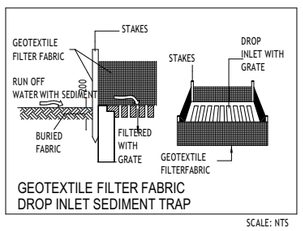


GEOTEXTILE FILTER FABRIC DROP INLET SEDIMENT TRAP
SCALE: NTS

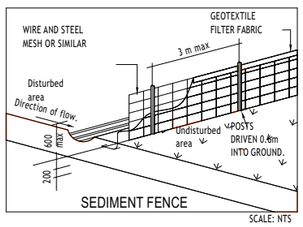


SEDIMENT FENCE
SCALE: NTS

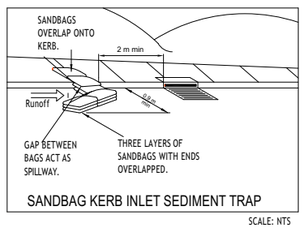


SANDBAG KERB INLET SEDIMENT TRAP
SCALE: NTS

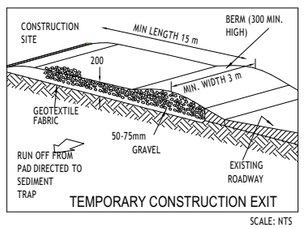


TEMPORARY CONSTRUCTION EXIT
SCALE: NTS

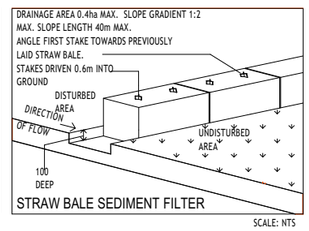

STRAW BALE SEDIMENT FILTER
SCALE: NTS

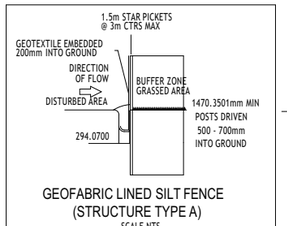

GEOFABRIC LINED SILT FENCE (STRUCTURE TYPE A)
SCALE NTS

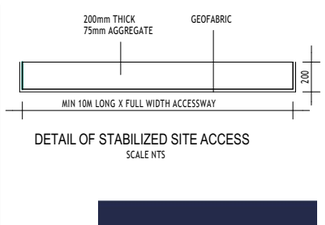

DETAIL OF STABILIZED SITE ACCESS
SCALE NTS

STONEGROVE HOMES

HIRA DESIGNS ©
This drawing remains the property of Hira Designs. It may be used for the purpose for which it was commissioned & in accordance with the terms of engagement for that commission.

Rev	Description	Date	App'd
-	CDC DRAWING ISSUED FOR APPROVAL	06.08.26	

Project
PROPOSED DOUBLE STOREY RESIDENCE

7 CATALANA STREET, SPRING FARM 2570
LOT 43, DP1316318

HIRA DESIGNS
Business Address: 13 Feathertop Ave, MINTO NSW 2566
Postal Address: 13 Feathertop Ave, MINTO NSW 2566
Phone Number: 0415112594
Email: info@hiradesigns.com.au
Project Designer:
Pramila Maharjan

Drawing Title
CDC DRAWINGS
SEDIMENT & CONTROL PLAN


Checked/Approved
PM

Scale
1:200 @A3 Sheet Size


Project Number
475041

Drawing Number Revision
CDC-110 -


Status
CDC DRAWINGS

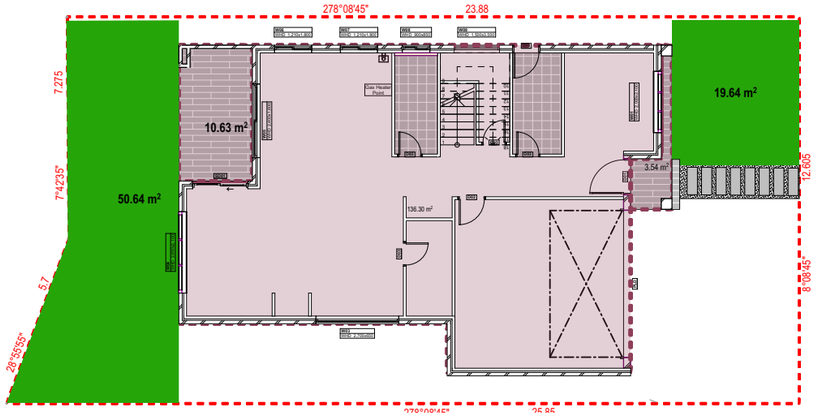


GROUND FLOOR BUILT UP AREA 1:200

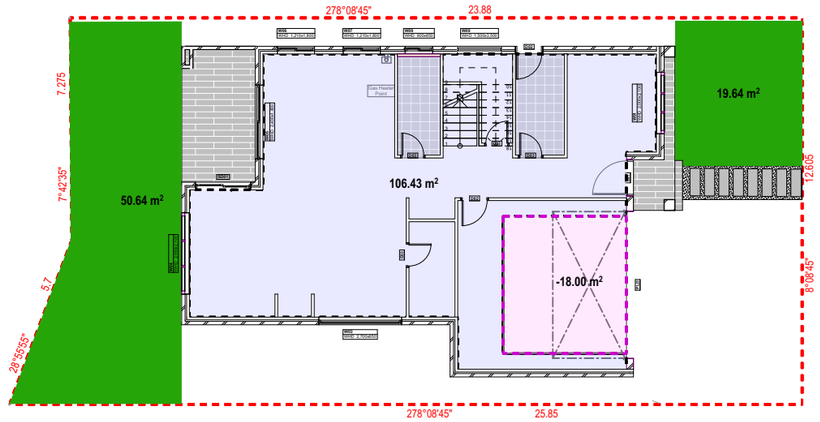

GROUND FLOOR GFA 1:200

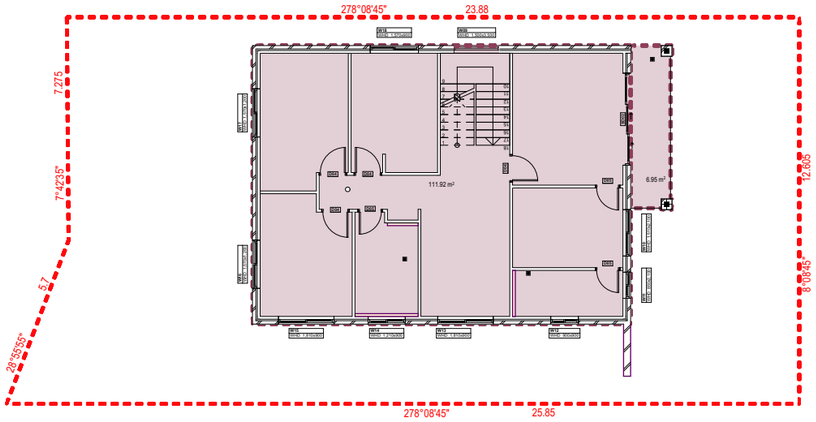

FIRST FLOOR BUILT UP AREA 1:200

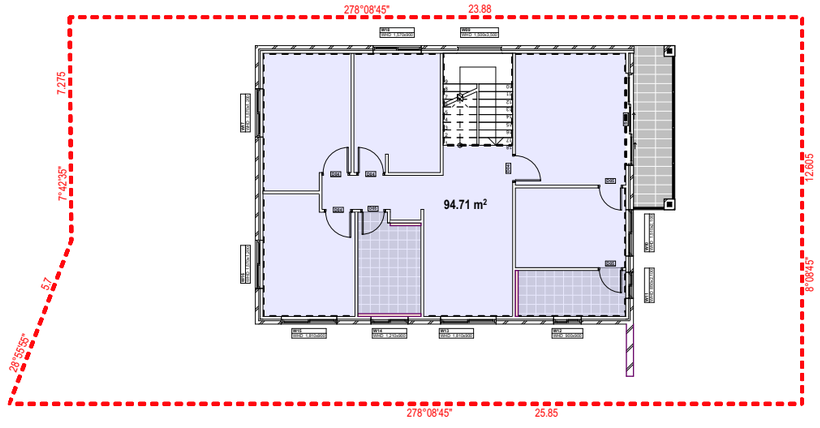

FIRST FLOOR GFA 1:200

DEVELOPMENT CALCULATIONS:

SITE AREA =305.9m²

GFA CALCULATION

PROPOSED GROUND FLOOR	=106.43m²
PROPOSED FIRST FLOOR	=94.71m²
TOTAL FLOOR AREA	**=201.14m²**
TOTAL GFA REQUIRED	=235m²
TOTAL GFA PROPOSED	**=106.43m²+94.71m²**
	=201.14m² (COMPLIES)

SITE COVER & LANDSCAPE CALCULATION

MINIMUM LANDSCAPE AREA REQUIRED	=15% OF 305.9m² = 45.885m²
PROPOSED LANDSCAPE AREA	**=51.06+20.03m² = 71.09m² COMPLIES**
LANDSCAPE AREA BEHIND THE BUILDING LINE (50% OF REQUIRED LANDSCAPE = 22.943m²)	**=51.06m² COMPLIES**
LANDSCAPE AREA FORWARD BUILDING LINE (25% OF REQUIRED LANDSCAPE = 11.47m²)	**=21.03m² COMPLIES**
P.O.S REQUIRED (24m²)	**=24m² COMPLIES**

SETBACKS

FRONT SETBACK (REQ. 4.5m)	**=4.50m COMPLIES**
FRONT SETBACK TO GARAGE (REQ. 5.5m)	**=5.50m COMPLIES**
REAR SETBACK GROUND FLOOR (REQ. 3.0m)	
REAR SETBACK TO ALFRESCO	**=3.652m COMPLIES**
REAR SETBACK TO BUILDING	**=5.619m COMPLIES**
FIRST FLOOR (REQ. 6.0m)	**=6.05m COMPLIES**
SIDE SETBACK SIDE A = 0.9m (GF) & 0.9m (FF),	**=0.9m & 0.925m COMPLIES**
SIDE B =0.9m(GF) &1.2m(FF)	**=1.625m & 0.925m COMPLIES**
HEIGHT RESTRICTION 8.5m MAX	<8.5m

Sydney Wide Certifiers Pty Ltd
Complying Development Certificate
Reference: SWC262403/01
Date: 13/10/2026
Sandres Markhani BDC05035

BUILT UP AREA CALCULATION

TOTAL SITE AREA	**305.91m²**
	PROPOSED
DWELLING	
GROUND FLOOR AREA	136.30m² (Garage Included)
PORCH	3.54m²
ALFRESCO	10.63m²
FIRST FLOOR	111.92m² (All void included)
BALCONY	7.22m²
TOTAL BUILT AREA	**269.69m² =29.03 sq**

Copyright HIRA DESIGNS ©

Notes
1. CONTRACTOR MUST VERIFY ALL DIMENSIONS ON SITE BEFORE COMMENCING WORK OR PREPARING SHOP DRAWINGS.
2. DO NOT SCALE DRAWINGS.
3. CONTRACTOR TO CHECK UNDERGROUND SERVICES BEFORE COMMENCING WORKS BY CONTACTING DIAL BEFORE YOU DIG. IF DIAL BEFORE YOU DIG INFORMATION IS PROVIDED WITH THIS DOCUMENTATION IT SHALL BE ASSUMED NOT TO BE CURRENT AND CONTRACTOR SHALL MAKE THEIR OWN ENQUIRES.

Rev	Description	Date	App'd
-	CDC DRAWING ISSUED FOR APPROVAL	06.08.26	

Project
PROPOSED DOUBLE STOREY RESIDENCE
7 CATALANA STREET, SPRING FARM 2570
LOT 43, DP1316318

HIRA DESIGNS
Business Address: 13 Feathertop Ave, MINTO NSW 2566
Postal Address: 13 Feathertop Ave, MINTO NSW 2566
Phone Number: 0415112594
Email: info@hiradesigns.com.au
Project Designer:
Pramila Maharjan

Drawing Title
CDC DRAWINGS
GFA DIAGRAMS

Checked/Approved
PM

Scale
1:200 @A3 Sheet Size

Project Number
475041

Drawing Number Revision
CDC-109 -

Status
CDC DRAWINGS

STONEGROVE HOMES

HIRA DESIGNS ©
This drawing remains the property of Hira Designs. It may be used for the purpose for which it was commissioned & in accordance with the terms of engagement for that commission.

Copyright HIRA DESIGNS ©

Notes
1. CONTRACTOR MUST VERIFY ALL DIMENSIONS ON SITE BEFORE COMMENCING WORK OR PREPARING SHOP DRAWINGS.
2. DO NOT SCALE DRAWINGS.
3. CONTRACTOR TO CHECK UNDERGROUND SERVICES BEFORE COMMENCING WORKS BY CONTACTING DIAL BEFORE YOU DIG. IF DIAL BEFORE YOU DIG INFORMATION IS PROVIDED WITH THIS DOCUMENTATION IT SHALL BE ASSUMED NOT TO BE CURRENT AND CONTRACTOR SHALL MAKE THEIR OWN ENQUIRES.

BASIX CERTIFICATE NUMBER:1867928S

FIXTURES	
SHOWER HEAD	MIN. FLOW RATE OF >6<=7.5L/M PLUS SPRAY FORCE AND /OR COVERAGE TEST WITH MIN 4 STAR RATING
TOILET FLUSH	MIN. RATING OF 4 STAR
TAPS	MIN. RATING OF 3 STAR
BASIN TAPS	MIN. RATING OF 4 STAR
ALTERNATIVE WATER	RAIN WATER TANK OF ATLEAST 2000l

The applicant must a rainwater tank of at least 2000 litres on the site. This rainwater tank must meet, and be installed in accordance with, the requirements of all applicable regulatory authorities.
The applicant must configure the rainwater tank to collect rain runoff from at least 120 square metres of the roof area of the development (excluding the area of the roof which drains to any stormwater tank or private dam).

CONSTRUCTION	AREA- m2	ADDITIONAL REUIREMENT	OPTIONS TO ADDRESS THERMAL BRIDGING	OTHER SPECIFICATIONS
floor - concrete slab on ground, waffle pod slab.	99.1	nil;not specified	nil	
floor - above habitable rooms or mezzanine, particle board; frame: timber - untreated softwood..	72.41	nil;none	nil	
floor - suspended floor above garage, particle board; frame: timber - untreated softwood.	21.72	nil;fibreglass batts or roll	nil	
garage floor - concrete slab on ground, 30% cement substitute, waffle pod slab.	31.26	none	nil	
external wall: brick veneer; frame: timber - untreated softwood.	all external walls	2.44 (or 3.00 including construction);fibreglass batts or roll + reflective foil in the cavity	nil	wall colour: Medium (solar absorptance 0.48-0.7)
external garage wall: brick veneer; frame: timber - untreated softwood.	30	fibreglass batts or roll + reflective foil in the cavity	nil	
internal wall shared with garage: plasterboard; frame: timber - untreated softwood.	30	nil;fibreglass batts or roll	nil	
internal wall: plasterboard; frame: timber - untreated softwood.	265	none	nil	
ceiling and roof - flat ceiling / pitched roof, framed - concrete tiles , timber - untreated softwood.	163.84	ceiling: 5 (up), roof: foil/ sarking ;ceiling: fibreglass batts or roll; roof: foil/sarking.	nil	roof space ventilation: unventilated; roof colour: medium (solar absorptance 0.6-0.7); 0.5 to ô 1.0% of ceiling area uninsulated

NOTE: Insulation specified in this Certificate must be installed in accordance with the ABCB Housing Provisions (Part 13.2.2) of the National Construction Code.
NOTE: If the additional ceiling insulation listed in the table above is greater than R3.0, refer to the ABCB Housing Provisions (Part 13.2.3 (6)) of the National Construction Code.
NOTE: In some climate zones, insulation should be installed with due consideration of condensation and associated interaction with adjoining building materials.
NOTE: Thermal breaks must be installed in metal framed walls and applicable roofs in accordance with the ABCB Housing Provisions of the National Construction Code.

WINDOW SCHEDULE

Window/door number	Orientation	Maxmium height(mm)	Maximum Width(mm)	Frame and glass specification	Shading Device	Overshadowing
W06	N	1800.00	1210.00	aluminium, single glazed (U- value: <=6.5, SHGC: 0.74 - 0.90)	none	not overshadowed
W07	N	1800.00	1210.00	aluminium, single glazed (U- value: <=6.5, SHGC: 0.74 - 0.90)	none	not overshadowed
W08	N	850.00	900.00	aluminium, single glazed (U- value: <=6.5, SHGC: 0.74 - 0.90)	none	not overshadowed
W09	N	3600.00	1500.00	aluminium, single glazed (U- value: <=6.5, SHGC: 0.74 - 0.90)	eave 450 mm, 150 mm above head of window or glazed door	not overshadowed
SD01	N	2400.00	1800.00	aluminium, single glazed (U- value: <=6.5, SHGC: 0.74 - 0.90)	eave 4430 mm, 300 mm above head of window or glazed door	2-4 m high, 2-5 m away
W18	N	900.00	1570.00	aluminium, single glazed (U- value: <=6.5, SHGC: 0.74 - 0.90)	eave 450 mm, 150 mm above head of window or glazed door	not overshadowed
SD02	E	2400.00	3000.00	aluminium, single glazed (U- value: <=6.5, SHGC: 0.74 - 0.90)	eave 1350 mm, 150 mm above head of window or glazed door	not overshadowed
W01	E	2100.00	2000.00	aluminium, single glazed (U- value: <=6.5, SHGC: 0.74 - 0.90)	eave 350 mm, 300 mm above head of window or glazed door	not overshadowed
W10	E	2100.00	1510.00	aluminium, single glazed (U- value: <=6.5, SHGC: 0.74 - 0.90)	eave 450 mm, 150 mm above head of window or glazed door	not overshadowed
W11	E	2100.00	850.00	aluminium, single glazed (U- value: <=6.5, SHGC: 0.74 - 0.90)	eave 450 mm, 150 mm above head of window or glazed door	not overshadowed
W03	S	650.00	2700.00	aluminium, single glazed (U- value: <=6.5, SHGC: 0.74 - 0.90)	none	not overshadowed
W12	S	900.00	900.00	aluminium, single glazed (U- value: <=6.5, SHGC: 0.74 - 0.90)	eave 450 mm, 150 mm above head of window or glazed door	not overshadowed
W13	S	900.00	1810.00	aluminium, single glazed (U- value: <=6.5, SHGC: 0.74 - 0.90)	eave 450 mm, 150 mm above head of window or glazed door	not overshadowed
W14	S	900.00	1210.00	aluminium, single glazed (U- value: <=6.5, SHGC: 0.74 - 0.90)	eave 450 mm, 150 mm above head of window or glazed door	not overshadowed
W15	S	900.00	1810.00	aluminium, single glazed (U- value: <=6.5, SHGC: 0.74 - 0.90)	eave 450 mm, 150 mm above head of window or glazed door	not overshadowed
W04	W	2100.00	2650.00	aluminium, single glazed (U- value: <=6.5, SHGC: 0.74 - 0.90)	eave 450 mm, 900 mm above head of window or glazed door	not overshadowed
W05	W	1800.00	2400.00	aluminium, single glazed (U- value: <=6.5, SHGC: 0.74 - 0.90)	eave 2400 mm, 900 mm above head of window or glazed door	not overshadowed
	W	1200.00	1510.00	aluminium, single glazed (U- value: <=6.5, SHGC: 0.74 - 0.90)	eave 450 mm, 150 mm above head of window or glazed door	not overshadowed
	W	1200.00	1570.00	aluminium, single glazed (U- value: <=6.5, SHGC: 0.74 - 0.90)	eave 450 mm, 150 mm above head of window or glazed door	not overshadowed

Sydney Wide Certifiers Pty Ltd
Complying Development Certificate
Reference: SWC262403/01
Date: 13/10/2026
Sandres Markhani BDC05035

Rev	Description	Date	App'd
-	CDC DRAWING ISSUED FOR APPROVAL	06.08.26	

Project
PROPOSED DOUBLE STOREY RESIDENCE

7 CATALANA STREET, SPRING FARM 2570
LOT 43, DP1316318

HIRA DESIGNS
Business Address: 13 Feathertop Ave, MINTO NSW 2566
Postal Address: 13 Feathertop Ave, MINTO NSW 2566
Phone Number: 0415112594
Email: info@hiradesigns.com.au
Project Designer:
Pramila Maharjan

Drawing Title
CDC DRAWINGS
BASIX COMMITMENTS SHEET

Checked/Approved
PM

Scale
@A3 Sheet Size

Project Number
475041

Drawing Number Revision
CDC-113 -

Status
CDC DRAWINGS

STONEGROVE HOMES

HIRA DESIGNS ©
This drawing remains the property of Hira Designs. It may be used for the purpose for which it was commissioned & in accordance with the terms of engagement for that commission.

Note:-
Landscape Plan to be read together with Architectural Plans
Refer to Architectural Plans for pavements, walls, steps, fence & levels
Refer to Architectural Plans for setback information
Refer to Engineer's Drawings for Hydraulic information
All levels are to be verified by Contractor on site .
Refer to Survey plan for detailed levels.
All landscape works be in strict accordance with Council's landscape code and guidelines

LANDSCAPE TO BE DONE BY OWNER AFTER HANDOVER

LEGEND	
Ref.img	Name
	Tree
	Shrub
	Grass (Landscape Area)
	Aggregate

GE:- GARDEN EDGING AS SELECTED
TREATED PINE SPLITS 90 MM 2.4 MT LENGTH, FASTENED TO HARWOOD STAKES, MIMIMUM DEPTH IN GROUND OF 300 MM WITH GALVANISED TREATED PINE SCREWS(SIZE 75 MM X 8G)


LAWN:- BUFFALO WITH SHIRLEYS NO.17 FERTILISER
ALL PLANTS TO HAVE 35 MM OF BARK CHIP MULCH SPREAD OVER TOP SOIL TURF TO BE WATERED MORNING AND EVENING FOR A PERIOD OF TWO WEEKS OR AD NECESSARY.

LANDSCAPE SCHEDULE

Refrence Image	ABB	COMMON NAME	BOTANICAL NAME	TYPE	HEIGHT	POT. SIZE	QUA.
	MG	Teddybear	Magnolia Grandiflora	Tree	4-6m	45l	1
	TCA	Tuckeroo	Cupaniopsis Anacardiodies	Tree	6-8m	45l	1
	SR	Lilly Pilly	Syzygium 'Resilience	SR	Trim	200mm	7
	HM	English Lavender	Lavandulaangustifolia	Shurb	Trim	200mm	As req.
	Turf	Buffalo Turf	Stenotaphrum Secundatum	Turf			

Copyright HIRA DESIGNS ©

Notes
1. CONTRACTOR MUST VERIFY ALL DIMENSIONS ON SITE BEFORE COMMENCING WORK OR PREPARING SHOP DRAWINGS.
2. DO NOT SCALE DRAWINGS.
3. CONTRACTOR TO CHECK UNDERGROUND SERVICES BEFORE COMMENCING WORKS BY CONTACTING DIAL BEFORE YOU DIG. IF DIAL BEFORE YOU DIG INFORMATION IS PROVIDED WITH THIS DOCUMENTATION IT SHALL BE ASSUMED NOT TO BE CURRENT AND CONTRACTOR SHALL MAKE THEIR OWN ENQUIRES.

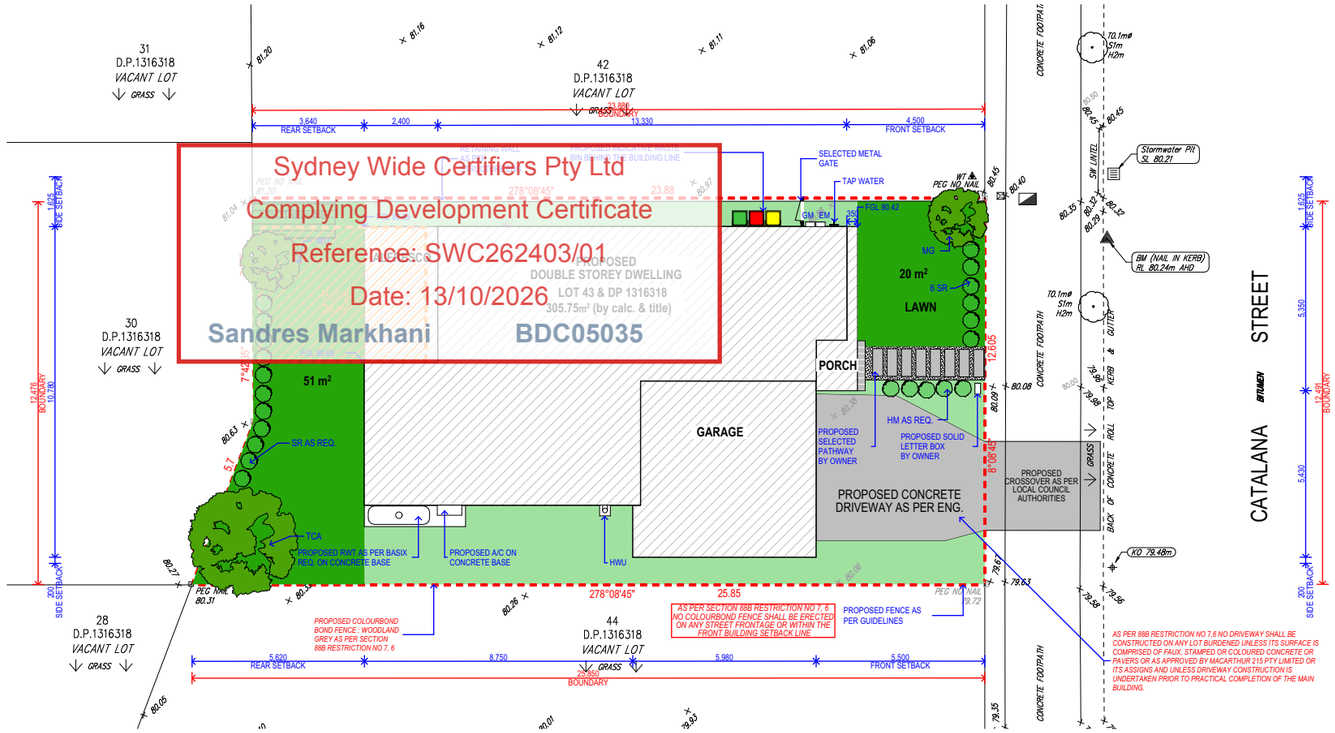

LANDSCAPE 1:200

HIRA DESIGNS ©
This drawing remains the property of Hira Designs. It may be used for the purpose for which it was commissioned & in accordance with the terms of engagement for that commission.

Rev	Description	Date	App'd
-	CDC DRAWING ISSUED FOR APPROVAL	06.08.26	

Project
PROPOSED DOUBLE STOREY RESIDENCE

7 CATALANA STREET, SPRING FARM 2570
LOT 43, DP1316318

HIRA DESIGNS
Business Address: 13 Feathertop Ave, MINTO NSW 2566
Postal Address: 13 Feathertop Ave, MINTO NSW 2566
Phone Number: 0415112594
Email: info@hiradesigns.com.au
Project Designer:
Pramila Maharjan

Drawing Title
CDC DRAWINGS
LANDSCAPE PLAN

Checked/Approved
PM

Scale
1:200 @A3 Sheet Size

Project Number
475041

Drawing Number Revision
CDC-114 -

Status
CDC DRAWINGS

STONEGROVE HOMES

Copyright HIRA DESIGNS ©

Notes
1. CONTRACTOR MUST VERIFY ALL DIMENSIONS ON SITE BEFORE COMMENCING WORK OR PREPARING SHOP DRAWINGS.
2. DO NOT SCALE DRAWINGS.
3. CONTRACTOR TO CHECK UNDERGROUND SERVICES BEFORE COMMENCING WORKS BY CONTACTING DIAL BEFORE YOU DIG. IF DIAL BEFORE YOU DIG INFORMATION IS PROVIDED WITH THIS DOCUMENTATION IT SHALL BE ASSUMED NOT TO BE CURRENT AND CONTRACTOR SHALL MAKE THEIR OWN ENQUIRES.

SPECIFICATION NOTES
PLANTING MATERIALS

Planting Mix:
Imported planting mix to planting beds is to comprise an approved soil mix of:

- 60% Soil mix (75% coarse sand and 25% blacksoil)
- 10% Mushroom compost
- 10% Composted sawdust
- 10% Pine bark 10% Composted manure

Mulch:
Mulch shall mean Hort-Bark (15mm grade) , free from material derived from Privet , Willow, Poplar ,Coral trees , or other noxious weeds . Any mulch exceeding the 25mm grade shall be rejected / removed from the site . Graded pine bark mulch (ANL code MHB) to be supplied by Australian Native Landscapes Pty Ltd Phone (02) 9450 1444 , or approved equivalent .

Plant Material:
All plant material must be true to the species . No substitutes will be allowed . All plants shall be free of fungus and insect damage . All plants shall be healthy , well shaped , not soft or force grown and not root bound.

Turfed areas:
All new turfed areas are to be selected weed free Soft Leaf Buffalo . Turf shall be laid neatly butted with staggered joins, with adjacent surfaces and have even running falls to all drainage points.

All new turfed area shall have a minimum 150mm depth of weed free top soil , placed and levelled prior to .

PREPARATION AND HARDWORKS

Excavating for Spot Planting
To planting areas , excavate a hole for each plant large enough to provide not less than twice the depth and twice the diameter than the root ball of species to be planted.

Staking
Use durable hardwood, straight, free from knots or twists, pointed at one end. Drive stakes into the ground a minimum one third of their length, avoiding damage to the root system .
45 Litre trees in 2 x 38x38x1800mm Hardwood Stake with double Nylon tie TIES
Provide a 50mm wide Nylon webbing tie per stake , securely to the stakes , one tie at half the height of the main stem and the other as necessary to stabilise the plant.

Timber Edge
MATERIAL: Timber edging shall consist of:
Edging: 100 x 50mm hardwood
Pegs: 50 x 50 x 400mm hardwood.
Fastenings: to be 75x3 .75mm diam. galvanised nails
INSTALLATION: Setout alignment of timber edges on site for approval of Superintendent . Excavate
to approved alignment and place edge band within trench to peg locations . Install pegs and timber edge in accordance with details . All timber edging to with adjoining turf.
MAINTE NANCE / P LANT E S TAB L IS HME NT - Landscape Contractors to provide 13 weeks for maintenance / plant establishment period. Carry out recurrent works of a maintenance nature including, but not limited to, watering, mowing, weeding, rubbish removal , fertilising, pest and disease control, , staking and tying, replanting, cultivating, pruning, hedge clipping, top dressing , and keeping the site neat and tidy.

LANDSCAPE WORKS:

- Prior to commencement of site landscape works, remove all building rubbish and debris from the site, remove all weed growth and unwanted remnant plant material.
- All ground surfaces should be formed to final profiles. See separate Survey Plan.
- Incorporated composted green manure in a ration of 1 meter to 5 meters of site soil before planting out in areas of native planting, in front of building complex where exotic plant species are to be planted incorporate cow manure in same ratio to site soil.
- For areas behind retaining walls and where site soil has been significantly modified replace with an organic soil mix to a depth of at least 350mm.
- Check pH and make sure it is between 5.5-7.0.
- After planting fertilize non native areas with Organic Life fertilizer or Osmocote slow release fertilizer and in areas planted up with native species fertilize with low phosphate Osmocote
- Mulch planted up areas to a depth of 75mm with native leaf litter in areas outside the building complex and mulch to same depth with fine leaf pine bark in all planter boxes within the building complex
- Water plants in well

GARDEN EDGING:

Garden edging to be either timber, brick or concrete (as selected by the owner) the edges are to be laid in even curves and straight lines as shown on the plan. The top of the edge is finish flush with the adjacent turf and mulch levels.

MAINTENANCE:
All landscape works are to be maintained for a period of twelve months from the date of completion. This includes the following: -

Watering: Which is to be done once a week for 2 months, then once a fortnight for 8 months.


Weeds: Which are to be maintained and mulch replaced to maintain a depth of 50mm.

Mowing: Which is to be done at 2 weeks intervals during spring [illegible]

Pruning: Which is to be done to encourage shape and size. Any plants or turf which fails during this period, are to be replace at no extra cost.


PROTECTION OF TREES RETAINED ON AND ADJACENT TO SITE
Existing trees so indicated shall be retained. The trees shall be protected for the period of construction by the erection of a fence not less that 1800 high, set out 5 times the stem diameter of the tree, or 3 metres clear of the tree, which ever is greater. Where existing protection fencing exists, it shall be maintained. The protected zone within this fence shall not be interfered with in any way during construction; the protected area shall be mulched at the time of erection of the protection fences with leaf litter mulch to a thickness of 75mm and the fenced zone shall be regularly watered. Finishing landscape works within these areas shall be carried out on ground levels as found, with minimum cultivation. Provide similar protection to primary root zones of trees on adjoining properties where root zones project in the property.

Sydney Wide Certifiers Pty Ltd
Complying Development Certificate
Reference: SWC262403/01
Date: 13/10/2026
Sandres Markhani BDC05035

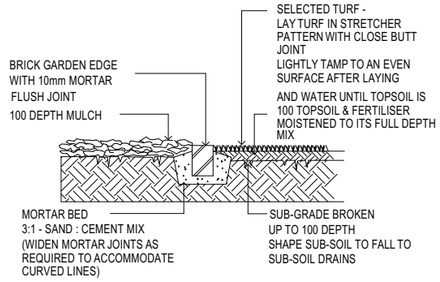

1. TURF & GARDEN EDGE DETAIL

NOTE :
ALIGNMENT OF BRICK EDGE SHALL BE EVEN & FREE FROM

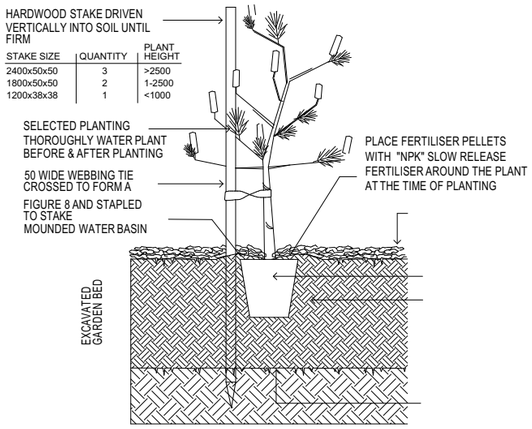

2. TREE & SHRUB PLANTING IN GARDEN BED

NOTE :
DO NOT PLANT IN UNSUITABLE WEATHER CONDITIONS SUCH AS EXTREME HEAT, COLD, WIND OR RAIN

Rev	Description	Date	App'd
-	CDC DRAWING ISSUED FOR APPROVAL	06.08.26	

Project
PROPOSED DOUBLE STOREY RESIDENCE

7 CATALANA STREET, SPRING FARM 2570
LOT 43, DP1316318

HIRA DESIGNS
Business Address: 13 Feathertop Ave, MINTO NSW 2566
Postal Address: 13 Feathertop Ave, MINTO NSW 2566
Phone Number: 0415112594
Email: info@hiradesigns.com.au
Project Designer:
Pramila Maharjan

Drawing Title
CDC DRAWINGS
LANDSCAPE NOTES

Checked/Approved
PM

Scale
@A3 Sheet Size

Project Number
475041

Drawing Number Revision
CDC-115 -

Status
CDC DRAWINGS

STONEGROVE HOMES

HIRA DESIGNS ©
This drawing remains the property of Hira Designs. It may be used for the purpose for which it was commissioned & in accordance with the terms of engagement for that commission.


Copyright HIRA DESIGNS ©

Notes
1. CONTRACTOR MUST VERIFY ALL DIMENSIONS ON SITE BEFORE COMMENCING WORK OR PREPARING SHOP DRAWINGS.
2. DO NOT SCALE DRAWINGS.
3. CONTRACTOR TO CHECK UNDERGROUND SERVICES BEFORE COMMENCING WORKS BY CONTACTING DIAL BEFORE YOU DIG. IF DIAL BEFORE YOU DIG INFORMATION IS PROVIDED WITH THIS DOCUMENTATION IT SHALL BE ASSUMED NOT TO BE CURRENT AND CONTRACTOR SHALL MAKE THEIR OWN ENQUIRES.



Sydney Wide Certifiers Pty Ltd
Complying Development Certificate
Reference: SWC262403/01
Date: 13/10/2026
Sandres Markhani BDC05035

MATERIALS SCHEDULE

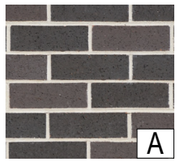

Brick (Dark & Stormy Thunder) or Similar



Render paint finish - 'Southerly' or similar



Aluminium windows & doors Powdercoat Black



Metal roof sheet - 'Colorbond Windspray or similar



Gutter downpipe- Apo grey or similar



Garage Door Dover White- Lincoln Panel or Similar

HIRA DESIGNS ©
This drawing remains the property of Hira Designs. It may be used for the purpose for which it was commissioned & in accordance with the terms of engagement for that commission.

Rev	Description	Date	App'd
-	CDC DRAWING ISSUED FOR APPROVAL	06.08.26	

Project
PROPOSED DOUBLE STOREY RESIDENCE

7 CATALANA STREET, SPRING FARM 2570
LOT 43, DP1316318

HIRA DESIGNS
Business Address: 13 Feathertop Ave, MINTO NSW 2566
Postal Address: 13 Feathertop Ave, MINTO NSW 2566
Phone Number: 0415112594
Email: info@hiradesigns.com.au
Project Designer:
Pramila Maharjan

Drawing Title
CDC DRAWINGS
FINISHES SCHEDULE

Checked/Approved
PM

Scale
@A3 Sheet Size

Project Number
475041

Drawing Number Revision
CDC-116 -

Status
CDC DRAWINGS

STONEGROVE HOMES