Compass Building Certification Pty Ltd
This document is referred to in:
Complying Development Certificate

COMPASS

Nick Georgopoulos *7/05/2022*

Accredited Certifier
Registration number 1925


CALCULATIONS (combined units)

TOTAL SITE AREA	=	638.49m²
GROUND FLOOR AREA	=	288.61m²
FIRST FLOOR AREA	=	196.01m²
GARAGE EXCLUSION	=	-36.00m²
TOTAL FLOOR AREA	=	448.62m²
LANDSCAPED AREA	=	224.00m²

Date	Purpose of Issue	Issue
NOV 2021	Issued for CDC	A
APR 2022	Issued for CDC	B

0007095970 04 Mar 2022
Assessor Abbas Chahrouzeh
Accreditation No. 101512
Address
12 Robertson Street ,
Merrylands , NSW, 2160
hstar.com.au

Compass Building Certification Pty Ltd
RECEIVED
05/05/2022
COMPASS

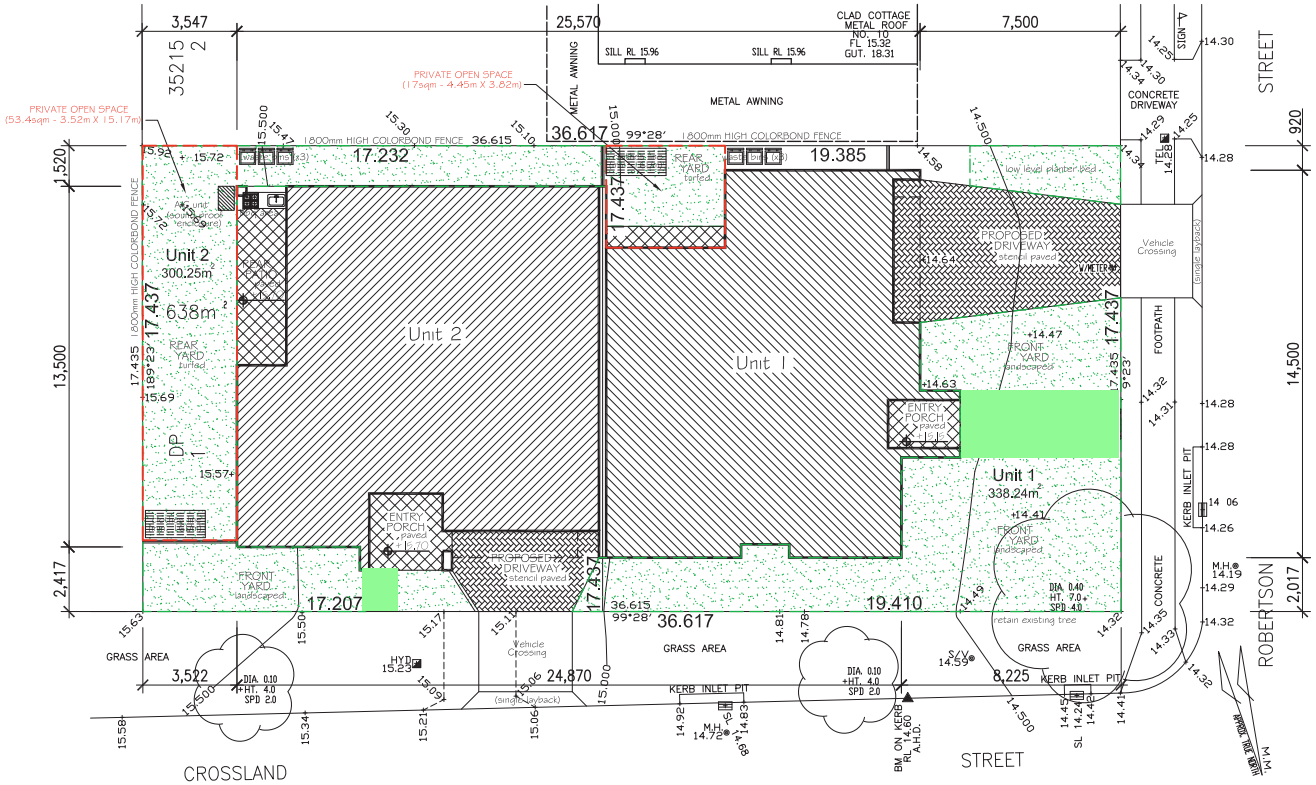

SITE / GROUND FLOOR PLAN

SCALE 1 : 200

P +61 2 9785 4677 I F +61 2 9785 4677
E info.ohaworkshop@gmail.com
Level 10 I 122 Arthur Street I North Sydney
N S W 2 0 6 1

Notes:
* Figured dimensions take precedence over scale drawings.
* Contractors to check and verify all levels, datum and dimensions on site.
* All materials and workmanship to be in accordance with current written manufacturers instructions, local regulations, and codes.
* All work to be carried out in a professional and workmanship like manner, according to the plans and the specifications

Project: Attached Dual Occupancy

Address: 12 Robertson Street, Merrylands

Client:

Drawing No: A001

Drawing Title: SITE PLAN and CALCULATIONS

Design By: OA
Drawn by: DD
Date: 22.11.2021
Scale: as shown @ A3

0 1 2 3 4 5

Project No.: 2194/21

Compass Building Certification Pty Ltd
This document is referred to in:
Complying Development Certificate

COMPASS


Nick Georgopoulos

7/05/2022

Accredited Certifier
Registration number 1925

Date	Purpose of Issue	Issue
NOV 2021	Issued for CDC	A
APR 2022	Issued for CDC	B

Compass Building Certification Pty Ltd
RECEIVED
05/05/2022
COMPASS

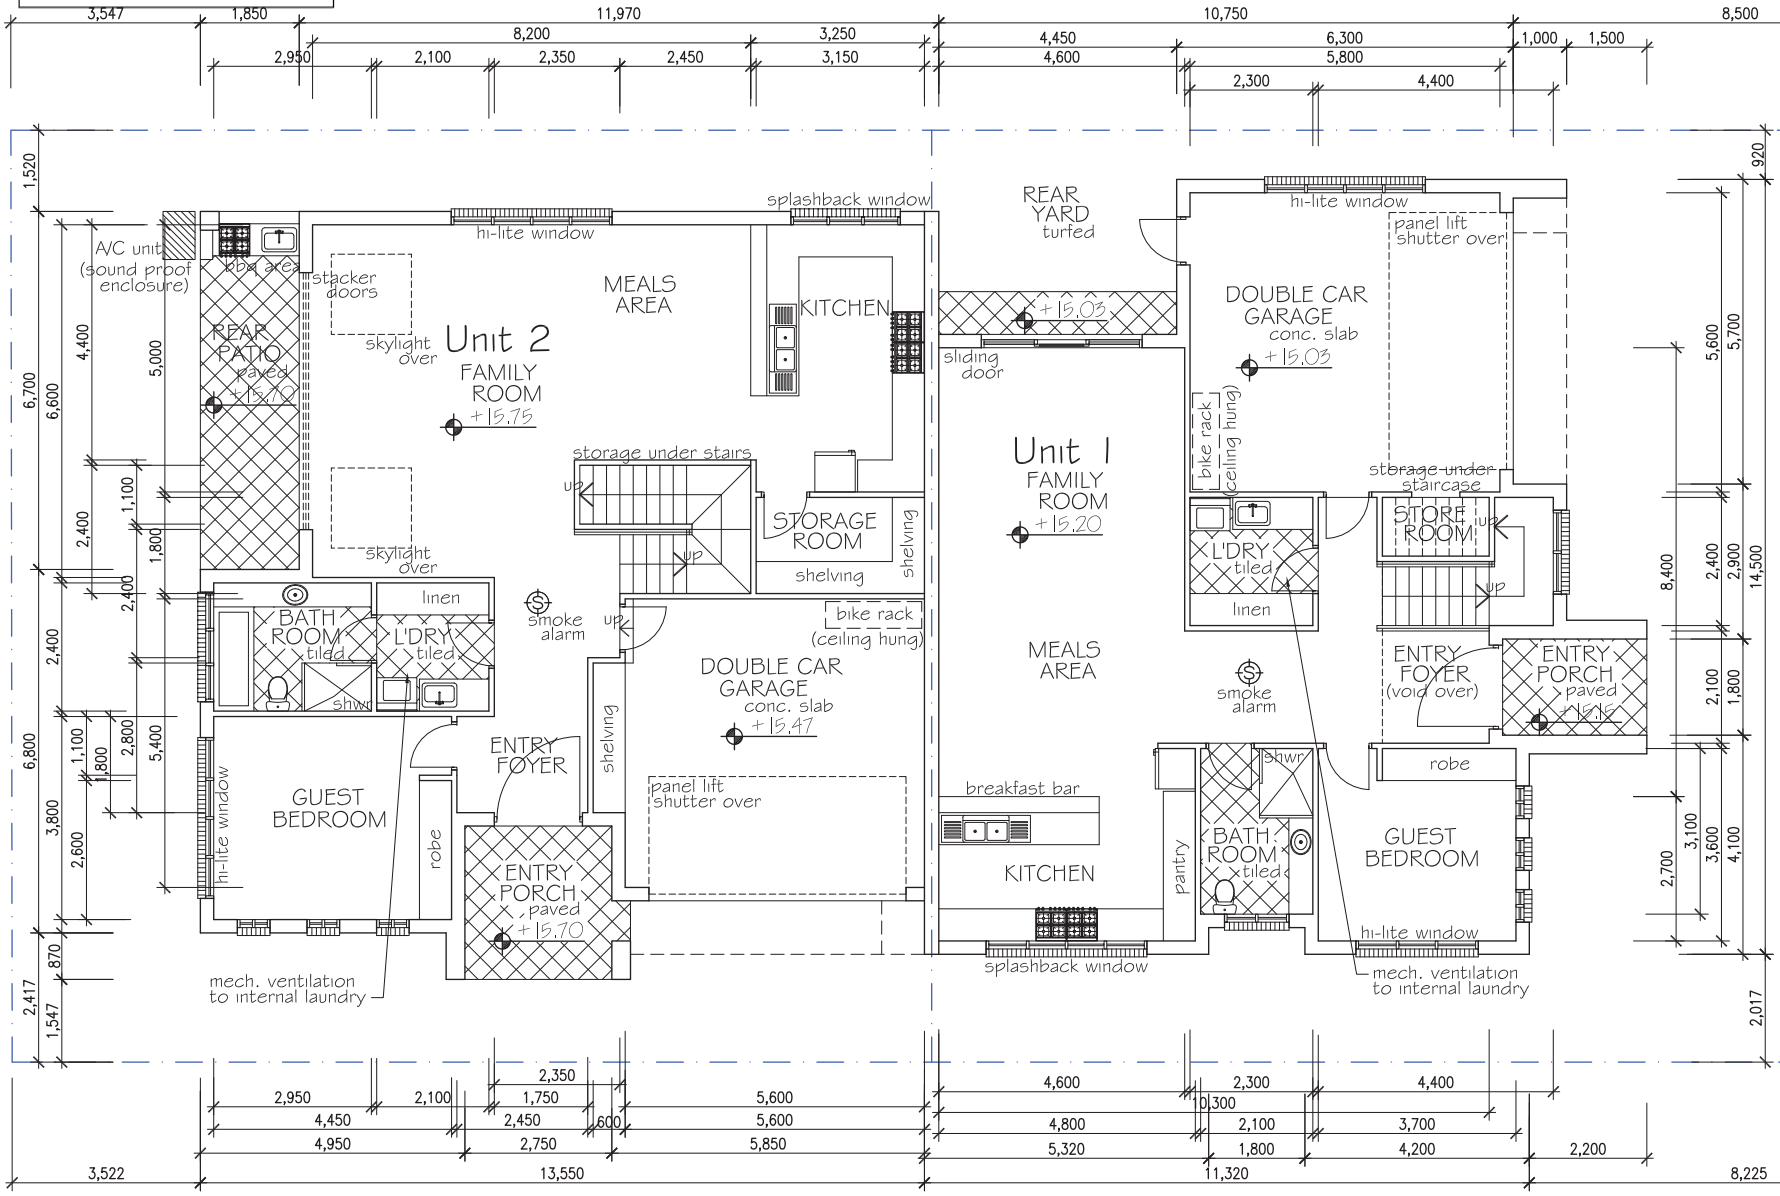

GROUND FLOOR PLAN

SCALE 1 : 100

P +61 2 9785 4677 | F +61 2 9785 4677
E info.ohaworkshop@gmail.com
Level 10 | 122 Arthur Street | North Sydney
N S W 2 0 6 1

Notes:

* Figured dimensions take precedence over scale drawings.
* Contractors to check and verify all levels, datum and dimensions on site.
* All materials and workmanship to be in accordance with current written manufacturers instructions, local regulations, and codes.
* All work to be carried out in a professional and workmanship like manner, according to the plans and the specifications

Project: Attached Dual Occupancy

Address: 12 Robertson Street, Merrylands

Client:

Drawing No: A002

Drawing Title: GROUND FLOOR PLAN

Design By: OA
Drawn by: DD
Date: 22.11.2021
Scale: as shown @ A3

0 1 2 3 4 5

Project No.: 2194/21


IMPORTANT NOTE:

BEDROOM WINDOWS ON FIRST FLOOR WHERE THE SILL HEIGHT IS LESS THAN 1.7m ABOVE THE FLOOR MUST BE PROTECTED BY A LOCKABLE DEVICE IN ACCORDANCE WITH PART 3.9.2.6 & PART 3.9.2.7 OF THE BCA / NCC

Compass Building Certification Pty Ltd
This document is referred to in:
Complying Development Certificate
COMPASS
Nick Georgopoulos
7/05/2022
Accredited Certifier
Registration number 1925

Compass Building Certification Pty Ltd
RECEIVED
05/05/2022
COMPASS

Date	Purpose of Issue	Issue
NOV 2021	Issued for CDC	A
APR 2022	Issued for CDC	B

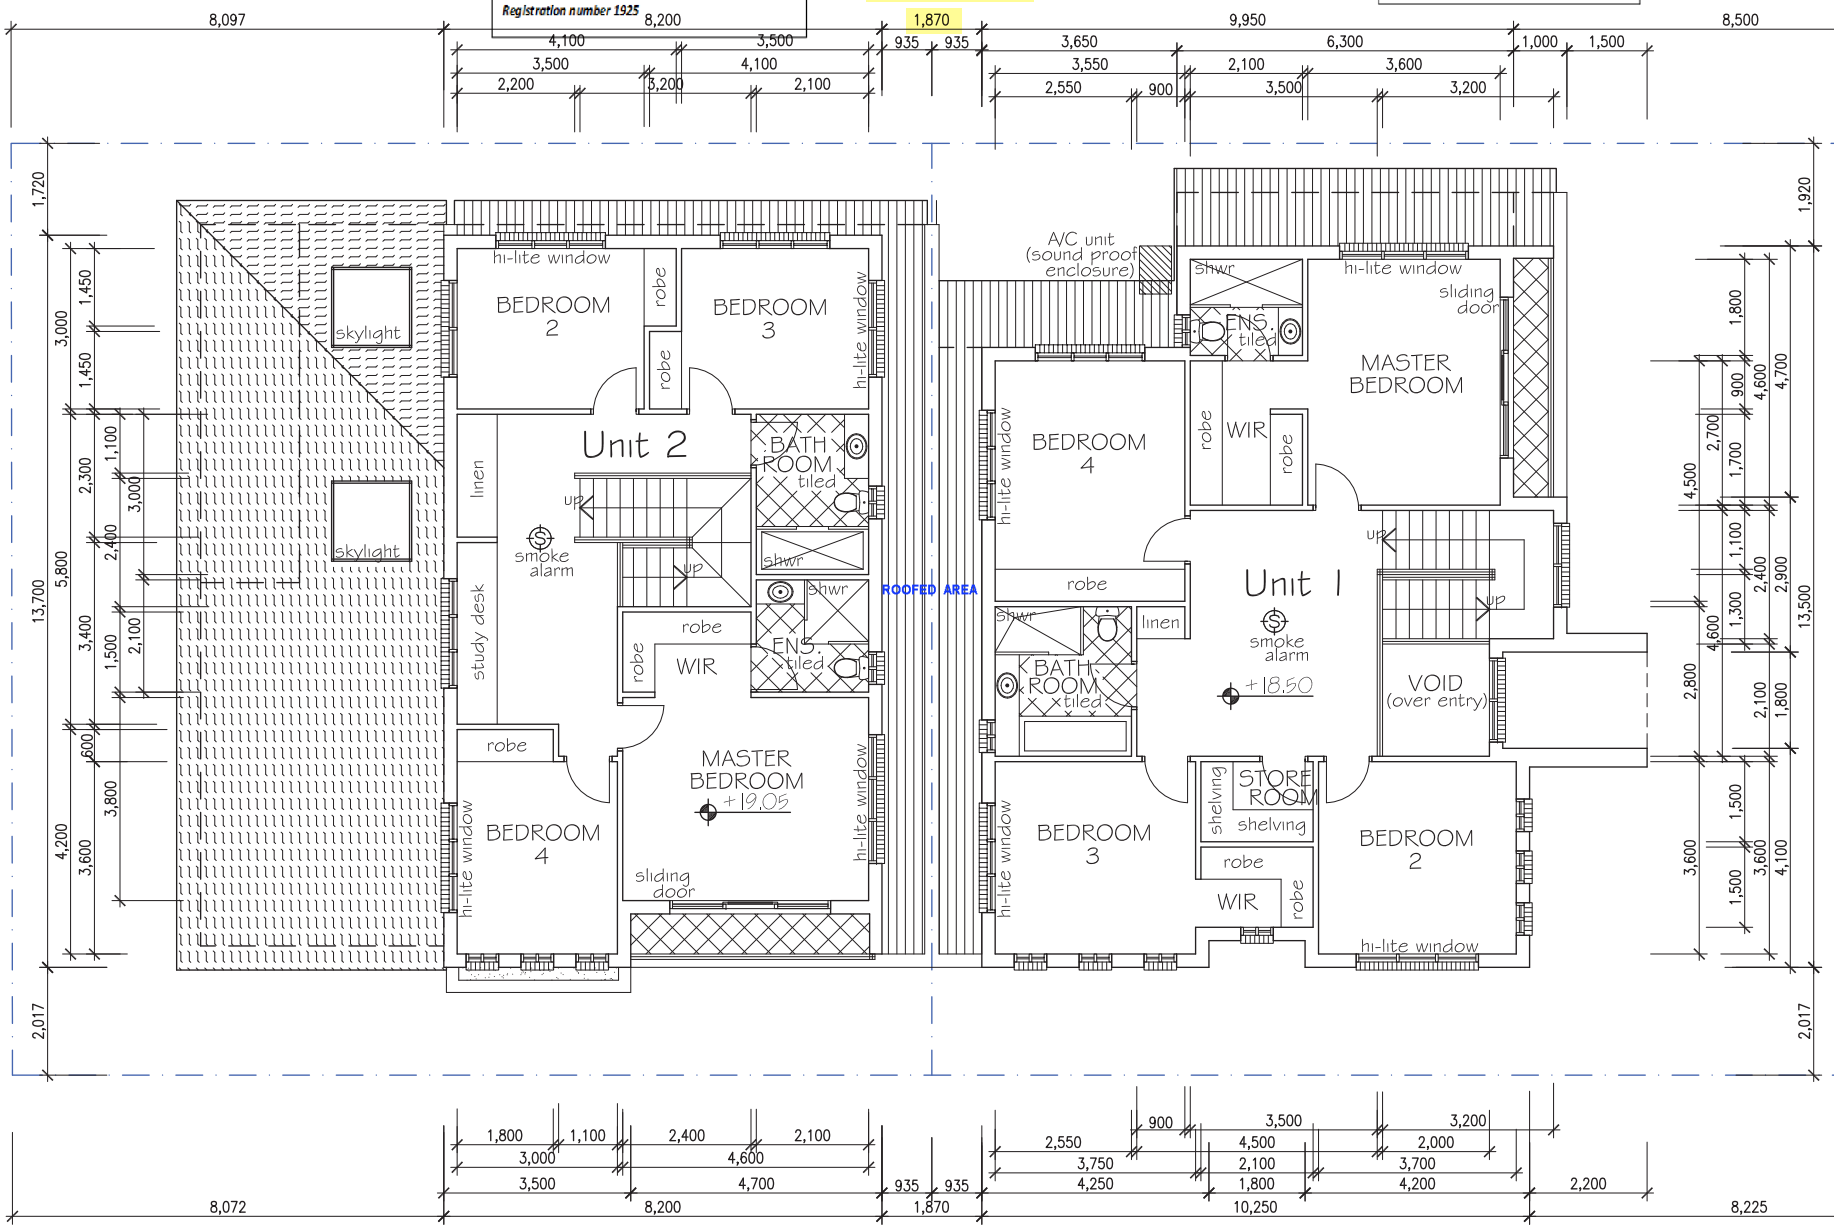

FIRST FLOOR PLAN

SCALE 1 : 100

P +61 2 9785 4677 | F +61 2 9785 4677
E info.ohaworkshop@gmail.com
Level 10 | 122 Arthur Street | North Sydney
N S W 2 0 6 1

Notes:

* Figured dimensions take precedence over scale drawings.
* Contractors to check and verify all levels, datum and dimensions on site.
* All materials and workmanship to be in accordance with current written manufacturers instructions, local regulations, and codes.
* All work to be carried out in a professional and workmanship like manner, according to the plans and the specifications

Project: Attached Dual Occupancy

Address: 12 Robertson Street, Merrylands

Client:


Drawing No: A003

Drawing Title: FIRST FLOOR PLAN

Design By: OA
Drawn by: DD
Date: 22.11.2021
Scale: as shown @ A3

0 1 2 3 4 5

Project No.: 2194/21

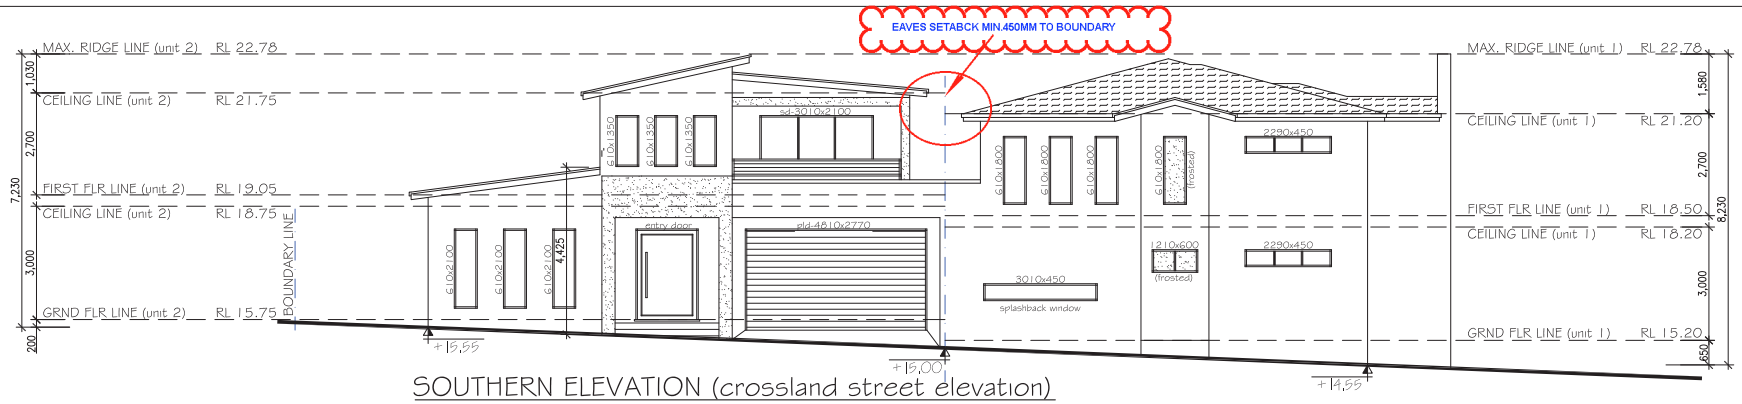


SOUTHERN ELEVATION (crossland street elevation)

SCALE 1 : 100




EASTERN ELEVATION (robertson street elevation)

SCALE 1 : 100

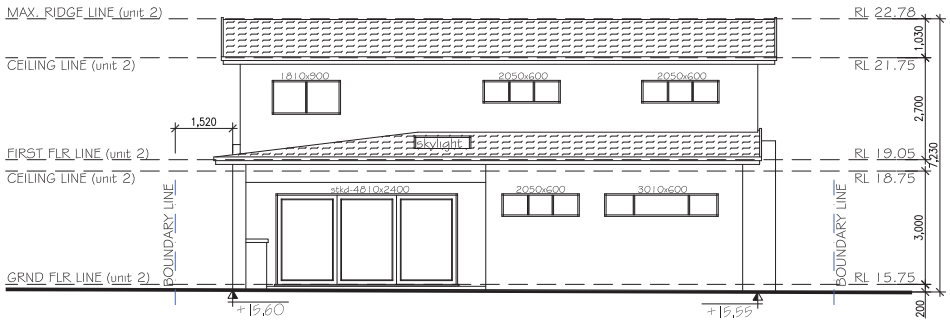

WESTERN ELEVATION

SCALE 1 : 100

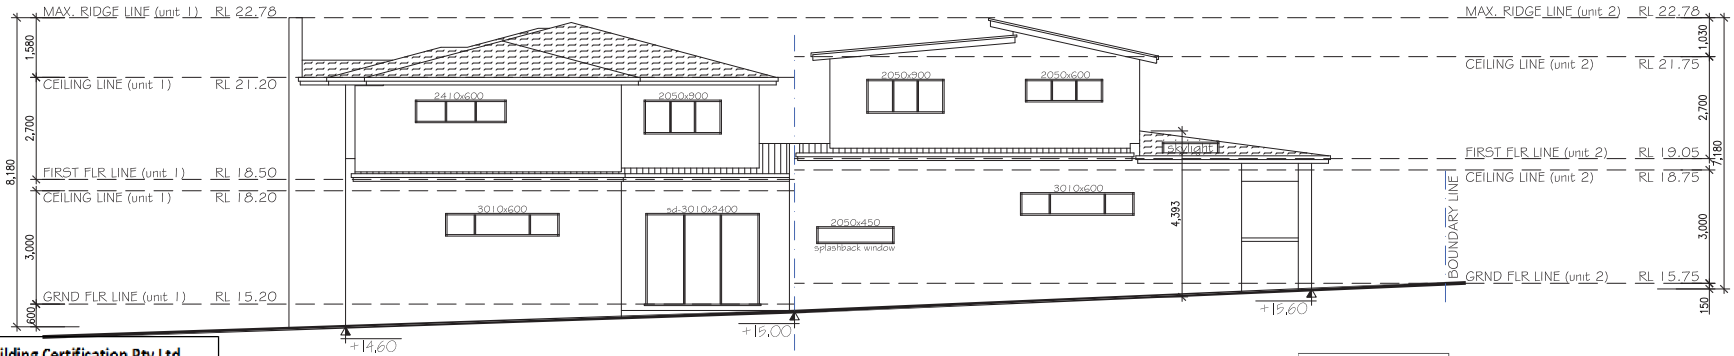

NORTHERN ELEVATION

SCALE 1 : 100

Date	Purpose of Issue	Issue
NOV 2021	Issued for CDC	A
APR 2022	Issued for CDC	B

P +61 2 9785 4677 I F +61 2 9785 4677
E info.ohaworkshop@gmail.com
Level 10 I 122 Arthur Street I North Sydney
N S W 2 0 6 1

Notes:

* Figured dimensions take precedence over scale drawings.
* Contractors to check and verify all levels, datum and dimensions on site.
* All materials and workmanship to be in accordance with current written manufacturers instructions, local regulations, and codes.
* All work to be carried out in a professional and workmanship like manner, according to the plans and the specifications

Project: Attached Dual Occupancy

Address: 12 Robertson Street, Merrylands

Client:

Drawing No: A005

Drawing Title: ELEVATIONS

Design By: OA
Drawn by: DD
Date: 22.11.2021
Scale: as shown @ A3

0 1 2 3 4 5


Project No.: 2194/21

Compass Building Certification Pty Ltd
This document is referred to in:
Complying Development Certificate
COMPASS
Nick Georgopoulos 7/05/2022
Accredited Certifier
Registration number 1925

Compass Building Certification Pty Ltd
RECEIVED
05/05/2022
COMPASS


IMPORTANT NOTE:
BEDROOM WINDOWS ON FIRST FLOOR WHERE THE SILL HEIGHT IS LESS THAN 1.7m ABOVE THE FLOOR MUST BE PROTECTED BY A LOCKABLE DEVICE IN ACCORDANCE WITH PART 3.9.2.6 & PART 3.9.2.7 OF THE BCA / NCC

Date	Purpose of Issue	Issue
NOV 2021	Issued for CDC	A
APR 2022	Issued for CDC	B

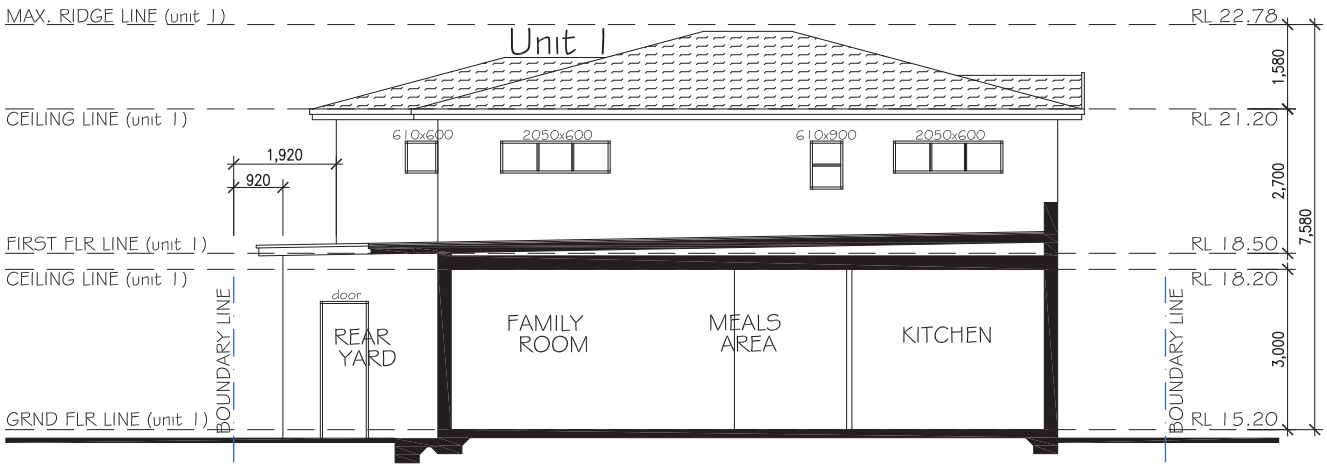

SECTION A-A / WESTERN ELEVATION (unit 1)

SCALE 1 : 100

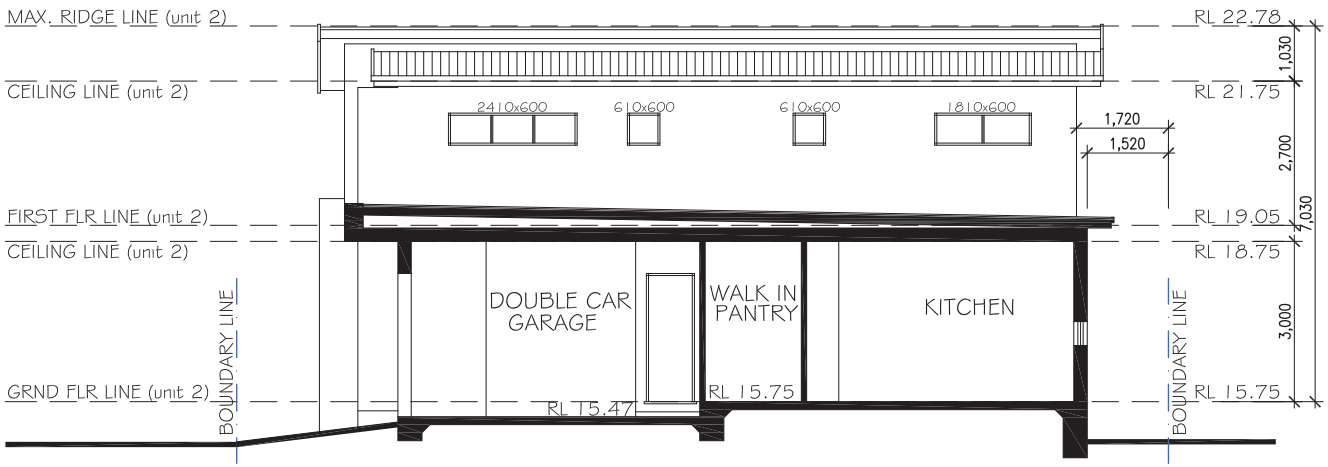

SECTION B-B / EASTERN ELEVATION (unit 2)

SCALE 1 : 100

IMPORTANT NOTE:

BEDROOM WINDOWS ON FIRST FLOOR WHERE THE SILL HEIGHT IS LESS THAN 1.7m ABOVE THE FLOOR MUST BE PROTECTED BY A LOCKABLE DEVICE IN ACCORDANCE WITH PART 3.9.2.6 & PART 3.9.2.7 OF THE BCA / NCC

Compass Building Certification Pty Ltd
This document is referred to in:
Complying Development Certificate

COMPASS

Nick Georgopoulos *7/05/2022*

Accredited Certifier
Registration number 1925

Compass Building Certification Pty Ltd

RECEIVED

05/05/2022

COMPASS

P +61 2 9785 4677 I F +61 2 9785 4677
E info.ohaworkshop@gmail.com
Level 10 I 122 Arthur Street I North Sydney
N S W 2 0 6 1

Notes:

* Figured dimensions take precedence over scale drawings.
* Contractors to check and verify all levels, datum and dimensions on site.
* All materials and workmanship to be in accordance with current written manufacturers instructions, local regulations, and codes.
* All work to be carried out in a professional and workmanship like manner, according to the plans and the specifications

Project: Attached Dual Occupancy

Address: 12 Robertson Street, Merrylands

Client:

Drawing No: A006

Drawing Title: SECTIONS


Design By: OA
Drawn by: DD
Date: 22.11.2021
Scale: as shown @ A3

0 1 2 3 4 5

Project No.: 2194/21

COLOURBOND ROOFING SHALL BE PROVIDED OVER CONCRETE ROOFED AREAS

Date	Purpose of Issue	Issue
NOV 2021	Issued for CDC	A
APR 2022	Issued for CDC	B

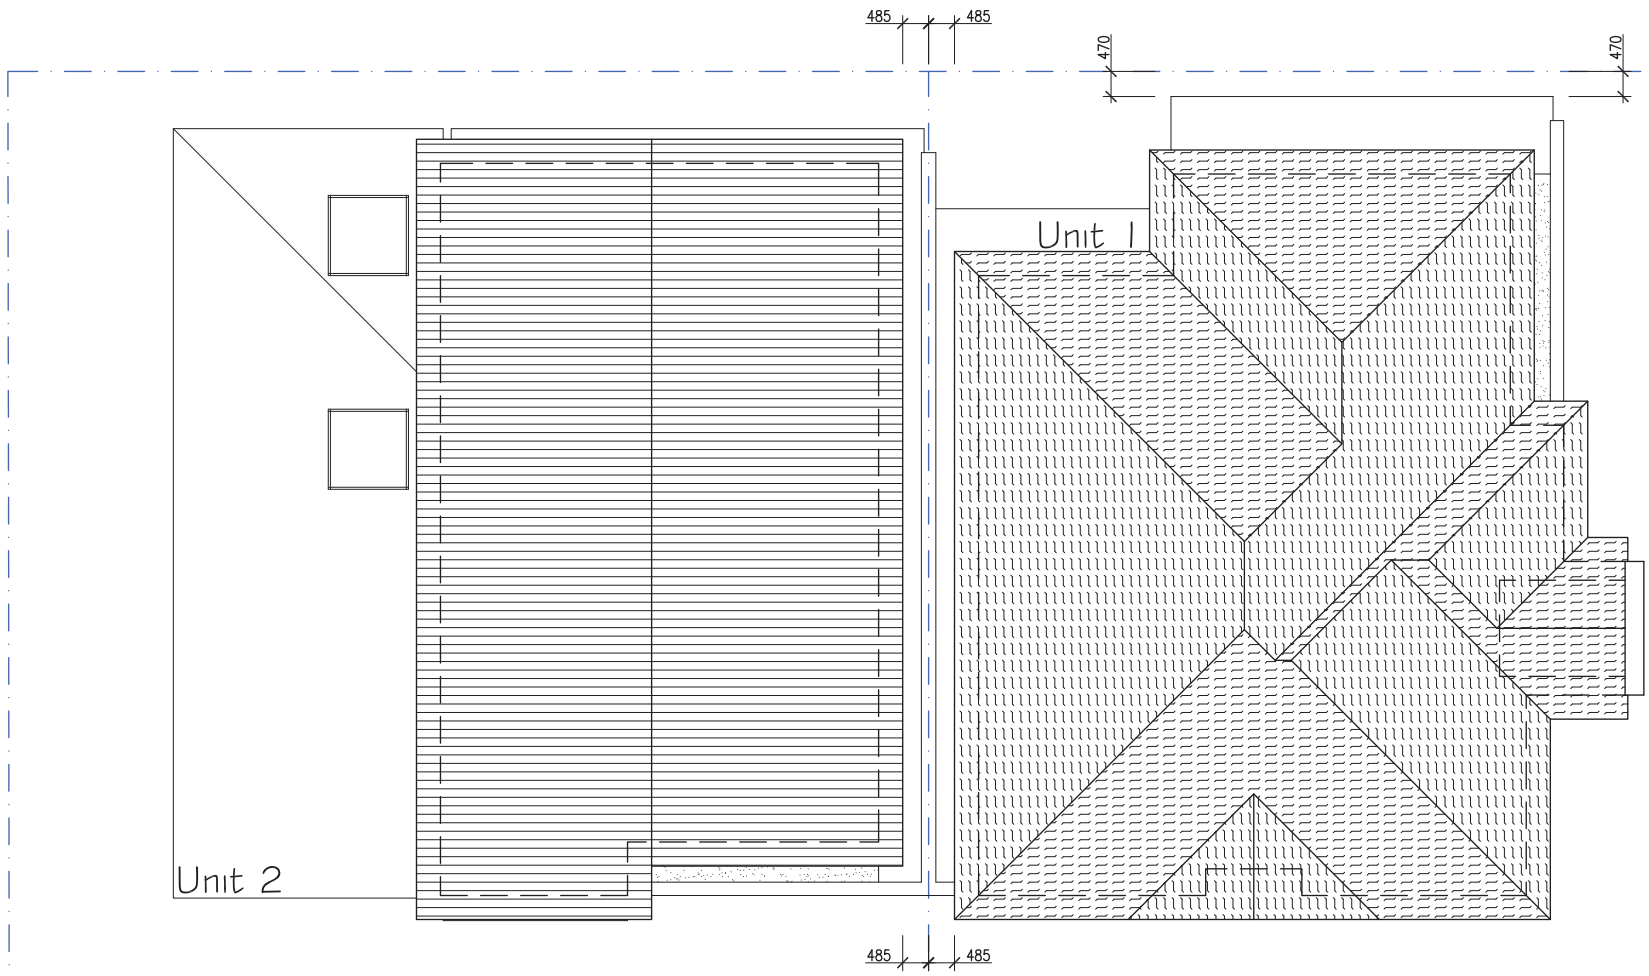

DETAILED ROOF PLAN

SCALE 1 : 100

Compass Building Certification Pty Ltd
RECEIVED
05/05/2022

P +61 2 9785 4677 I F +61 2 9785 4677
E info.ohaworkshop@gmail.com
Level 10 I 122 Arthur Street I North Sydney
N S W 2 0 6 1

Notes:
* Figured dimensions take precedence over scale drawings.
* Contractors to check and verify all levels, datum and dimensions on site.
* All materials and workmanship to be in accordance with current written manufacturers instructions, local regulations, and codes.
* All work to be carried out in a professional and workmanship like manner, according to the plans and the specifications

Project: Attached Dual Occupancy

Address: 12 Robertson Street, Merrylands

Client:

Drawing No: A004

Drawing Title: ROOF PLAN

Design By: OA
Drawn by: DD
Date: 22.11.2021
Scale: as shown @ A3

0 1 2 3 4 5

Project No.: 2194/21

Compass Building Certification Pty Ltd
This document is referred to in:
Complying Development Certificate
Nick Georgopoulos
7/05/2022
Accredited Certifier
Registration number 1925

Schedule of BASIX commitments (unit 1 and unit 2)
The commitments set out below regulate how the proposed development is to be carried out. It is a condition of any development consent granted, or complying development certificate issued, for the proposed development, that BASIX commitments be complied with.

1. Commitments for multi-dwelling houses

(a) Dwellings

(I) Water

(a) The applicant must comply with the commitments listed below in carrying out the development of a dwelling listed in a table below.

(b) The applicant must plant indigenous or low water use species of vegetation throughout the area of land specified for the dwelling in the "Indigenous species" column of the table below, as private landscaping for that dwelling. (This area of indigenous vegetation is to be contained within the "Area of garden and lawn" for the dwelling specified in the "Description of Project" table).

(c) If a rating is specified in the table below for a fixture or appliance to be installed in the dwelling, the applicant must ensure that each such fixture and appliance meets the rating specified for it.

(d) The applicant must install an on demand hot water recirculation system which regulates all hot water use throughout the dwelling, where indicated for a dwelling in the "HW recirculation or diversion" column of the table below.

(e) The applicant must install:

(aa) a hot water diversion system to all showers, kitchen sinks and all basins in the dwelling, where indicated for a dwelling in the "HW recirculation or diversion" column of the table below; and

(bb) a separate diversion tank (or tanks) connected to the hot water diversion systems of at least 100 litres. The applicant must connect the hot water diversion tank to all toilets in the dwelling.

(e) The applicant must not install a private swimming pool or spa for the dwelling, with a volume exceeding that specified for it in the table below.

(f) If specified in the table, that pool or spa (or both) must have a pool cover or shading (or both).

(g) The pool or spa must be located as specified in the table.

(h) The applicant must install, for the dwelling, each alternative water supply system, with the specified size, listed for that dwelling in the table below. Each system must be configured to collect run-off from the areas specified (excluding any area which supplies any other alternative water supply system), and to divert overflow as specified. Each system must be connected as specified.

(II) Energy

(a) The applicant must comply with the commitments listed below in carrying out the development of a dwelling listed in a table below.

(b) The applicant must install each hot water system specified for the dwelling in the table below, so that the dwelling's hot water is supplied by that system. If the table specifies a central hot water system for the dwelling, then the applicant must connect that central system to the dwelling, so that the dwelling's hot water is supplied by that central system.

(c) The applicant must install, in each bathroom, kitchen and laundry of the dwelling, the ventilation system specified for that room in the table below. Each such ventilation system must have the operation control specified for it in the table.

(d) The applicant must install the cooling and heating system/s specified for the dwelling under the "Living areas" and "Bedroom areas" headings of the "Cooling" and "Heating" columns in the table below, in/for at least 1 living/bedroom area of the dwelling. If no cooling or heating system is specified in the table for "Living areas" or "Bedroom areas", then no systems may be installed in any such areas. If the term "zoned" is specified beside an air conditioning system, then the system must provide for day/night zoning between living areas and bedrooms

(a) This commitment applies to each room or area of the dwelling which is referred to in a heading to the "Artificial lighting" column of the table below (but only to the extent specified for that room or area). The applicant must ensure that the "primary type of artificial lighting" for each such room in the dwelling is fluorescent lighting or light emitting diode (LED) lighting. If the term "dedicated" is specified for a particular room or area, then the light fittings in that room or area must only be capable of being used for fluorescent lighting or light emitting diode (LED) lighting.

(b) This commitment applies to each room or area of the dwelling which is referred to in a heading to the "Natural lighting" column of the table below (but only to the extent specified for that room or area). The applicant must ensure that each such room or area is fitted with a window and/or skylight.

(c) This commitment applies if the applicant installs a water heating system for the dwelling's pool or spa. The applicant must:

(aa) install the system specified for the pool in the "Individual Pool" column of the table below (or alternatively must not install any system for the pool). If specified, the applicant must install a timer, to control the pool's pump; and

(bb) install the system specified for the spa in the "Individual Spa" column of the table below (or alternatively must not install any system for the spa). If specified, the applicant must install a timer to control the spa's pump.

(h) The applicant must install in the dwelling:

(aa) the kitchen cook-top and oven specified for that dwelling in the "Appliances & other efficiency measures" column of the table below;

(bb) each appliance for which a rating is specified for that dwelling in the "Appliances & other efficiency measures" column of the table, and ensure that the appliance has that minimum rating; and

(cc) any clothes drying line specified for the dwelling in the "Appliances & other efficiency measures" column of the table.

(i) If specified in the table, the applicant must carry out the development so that each refrigerator space in the dwelling is "well ventilated".

(j) The applicant must install the photovoltaic system specified for the dwelling under the "Photovoltaic system" heading of the "Alternative energy" column of the table below, and connect the system to that dwelling's electrical system.

(III) Thermal Comfort

(a) The applicant must attach the certificate referred to under "Assessor details" on the front page of this BASIX certificate (the "Assessor Certificate") to the development application and construction certificate application for the proposed development (or, if the applicant is applying for a complying development certificate for the proposed development, to that application). The applicant must also attach the Assessor Certificate to the application for a final occupation certificate for the proposed development.

(b) The Assessor Certificate must have been issued by an Accredited Assessor in accordance with the Thermal Comfort Protocol.

(c) The details of the proposed development on the Assessor Certificate must be consistent with the details shown in this BASIX Certificate, including the details shown in the "Thermal Loads" table below.

(d) The applicant must show on the plans accompanying the development application for the proposed development, all matters which the Thermal Comfort Protocol requires to be shown on those plans. Those plans must bear a stamp of endorsement from the Accredited Assessor, to certify that this is the case.

Compass Building Certification Pty Ltd

RECEIVED

05/05/2022

COMPASS

.

(a) The applicant must show on the plans accompanying the application for a construction certificate (or complying development certificate, if applicable), all thermal performance specifications set out in the Assessor Certificate, and all aspects of the proposed development which were used to calculate those specifications.

(b) The applicant must construct the development in accordance with all thermal performance specifications set out in the Assessor Certificate, and in accordance with those aspects of the development application or application for a complying development certificate which were used to calculate those specifications.

(c) Where there is an in-slab heating or cooling system, the applicant must:

(aa) Install insulation with an R-value of not less than 1.0 around the vertical edges of the perimeter of the slab; or

(bb) On a suspended floor, install insulation with an R-value of not less than 1.0 underneath the slab and around the vertical edges of the perimeter of the slab.

(h) The applicant must construct the floors and walls of the development in accordance with the specifications listed in the table below.

3. Commitments for common areas and central systems/facilities for the development (non-building specific)

(b) Common areas and central systems/facilities

(I) Water

(a) If, in carrying out the development, the applicant installs a showerhead, toilet, tap or clothes washer into a common area, then that item must meet the specifications listed for it in the table.

(b) The applicant must install (or ensure that the development is serviced by) the alternative water supply system(s) specified in the "Central systems" column of the table below. In each case, the system must be sized, be configured, and be connected, as specified in the table.

(c) A swimming pool or spa listed in the table must not have a volume (in kLs) greater than that specified for the pool or spa in the table.

(d) A pool or spa listed in the table must have a cover or shading if specified for the pool or spa in the table.

(e) The applicant must install each fire sprinkler system listed in the table so that the system is configured as specified in the table.

(f) The applicant must ensure that the central cooling system for a cooling tower is configured as specified in the table.

(ii) Energy

(a) If, in carrying out the development, the applicant installs a ventilation system to service a common area specified in the table below, then that ventilation system must be of the type specified for that common area, and must meet the efficiency measure specified.

(b) In carrying out the development, the applicant must install, as the "primary type of artificial lighting" for each common area specified in the table below, the lighting specified for that common area. This lighting must meet the efficiency measure specified.

The applicant must also install a centralised lighting control system or Building Management System (BMS) for the common area, where specified.

(c) The applicant must install the systems and fixtures specified in the "Central energy systems" column of the table below. In each case, the system or fixture must be of the type, and meet the specifications, listed for it in the table.

1. In these commitments, "applicant" means the person carrying out the development.
2. The applicant must identify each dwelling, building and common area listed in this certificate, on the plans accompanying any development application, and on the plans and specifications accompanying the application for a construction certificate / complying development certificate, for the proposed development, using the same identifying letter or reference as is given to that dwelling, building or common area in this certificate.
3. This note applies if the proposed development involves the erection of a building for both residential and non-residential purposes (or the change of use of a building for both residential and non-residential purposes). Commitments in this certificate which are specified to apply to a "common area" of a building or the development, apply only to that part of the building or development to be used for residential purposes.
4. If this certificate lists a central system as a commitment for a dwelling or building, and that system will also service any other dwelling or building within the development, then that system need only be installed once (even if it is separately listed as a commitment for that other dwelling or building).
5. If a star or other rating is specified in a commitment, this is a minimum rating.
6. All alternative water systems to be installed under these commitments (if any), must be installed in accordance with the requirements of all applicable regulatory authorities. NOTE: NSW Health does not recommend that stormwater, recycled water or private dam water be used to irrigate edible plants which are consumed raw, or that rainwater be used for human consumption in areas with potable water supply.

Date	Purpose of Issue	Issue
NOV 2021	Issued for CDC	A
APR 2022	Issued for CDC	B





P +61 2 9785 4677 I F +61 2 9785 4677
E info.ohaworkshop@gmail.com
Level 10 I 122 Arthur Street I North Sydney
N S W 2 0 6 1

Notes:
* Figured dimensions take precedence over scale drawings.
* Contractors to check and verify all levels, datum and dimensions on site.
* All materials and workmanship to be in accordance with current written manufacturers instructions, local regulations, and codes.
* All work to be carried out in a professional and workmanship like manner, according to the plans and the specifications

Project:
Attached Dual Occupancy

Address:
12 Robertson Street, Merrylands

Client:
.

Drawing No:
A007

Drawing Title:
BASIX COMMITMENTS

Design By: OA
Drawn by: DD
Date: 22.11.2021
Scale: as shown @ A3

0 1 2 3 4 5

Project No:
2194/21

Compass Building Certification Pty Ltd


RECEIVED

05/05/2022

Date	Purpose of Issue	Issue
NOV 2021	Issued for CDC	A
APR 2022	Issued for CDC	B

CALCULATIONS

TOTAL SITE AREA	= 638.49m^2
Proposed Unit 1 Lot Area (fronting robertson street)	= 338.24m^2
Proposed Unit 2 Lot Area (frosting crossland street)	= 300.25m^2

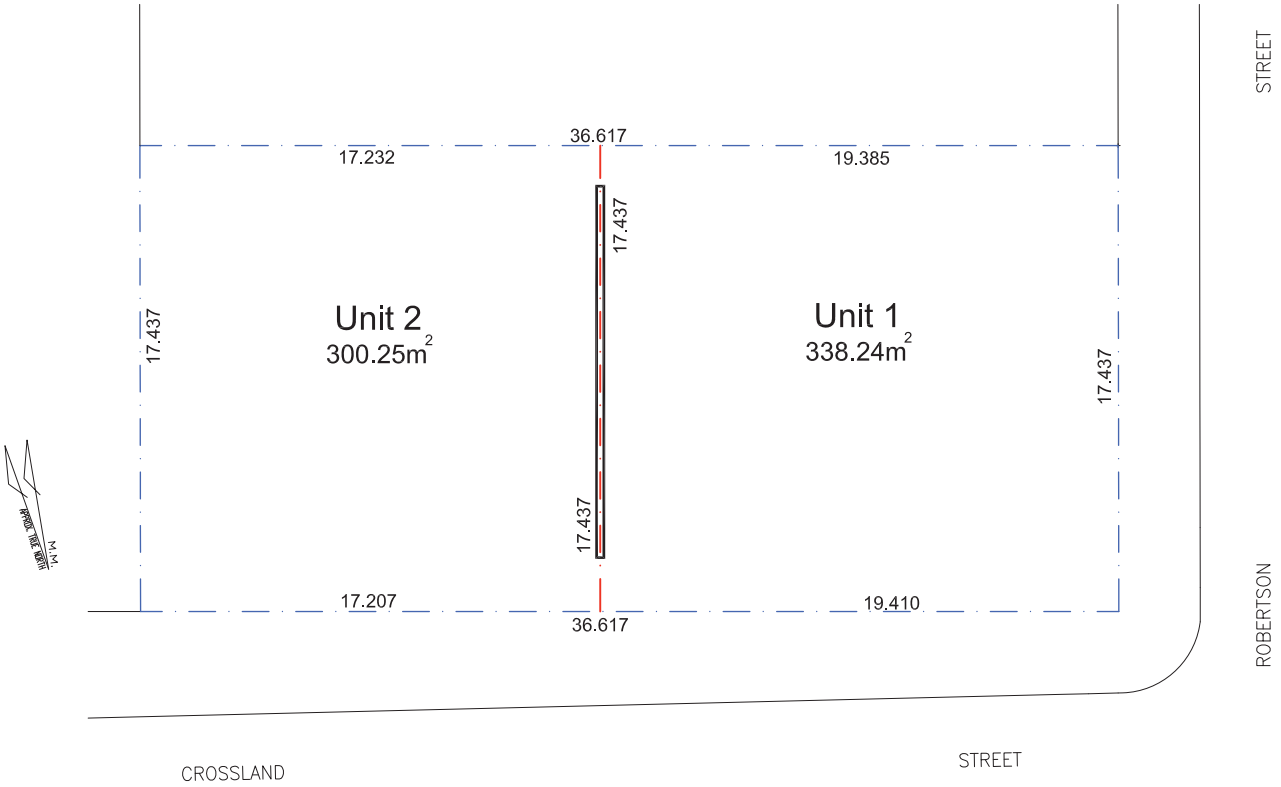

CONCEPT SUBDIVISION LINE (torrens title)

SCALE 1 : 200

P +61 2 9785 4677 I F +61 2 9785 4677
E info.ohaworkshop@gmail.com
Level 10 I 122 Arthur Street I North Sydney
N S W 2 0 6 1

Notes:

* Figured dimensions take precedence over scale drawings.
* Contractors to check and verify all levels, datum and dimensions on site.
* All materials and workmanship to be in accordance with current written manufacturers instructions, local regulations, and codes.
* All work to be carried out in a professional and workmanship like manner, according to the plans and the specifications

Project: Attached Dual Occupancy

Address: 12 Robertson Street, Merrylands

Client:

Drawing No: A008

Drawing Title: SUBDIVISION PLAN (concept)

Design By: OA
Drawn by: DD
Date: 22.11.2021
Scale: as shown @ A3

0 1 2 3 4 5

Project No.: 2194/21