FOR CONSTRUCTION

LOT 53 - 4 KILLEEN STREET AUBURN IN DP. 6713

ALTERATION & ADDITION TO EXISTING BUILDING AND CONSTRUCTION OF GRANNY FLAT



GENERAL LEGEND

AC	AIR CONDITIONING UNIT
AL	POWDERCOATED ALUMINIUM DOOR/ WINDOW TYPE
BAL	BALUSTRADE
BG	BOX GUTTER
BR1, BR2, etc.	BRICK FACE TYPE
CAP	METAL CAPPING
CD1, CD2, etc.	WALL CLADDING
CONC.	CONCRETE FLOOR
CPT	CARPET
CRT	CONCRETE ROOF TILES
CR1, CR2, etc.	CEMENT RENDER TYPE/ COLOUR
DP/S	DOWN PIPE
DW	DISH WASHER
ED	ENTRY DOOR
F	FRIDGE
FAS	FASCIA
FET	FEATURE TILE
FT, FT1, FT2, etc.	FLOOR TILES
FW	FLOOR WASTE
GD	GARAGE DOOR
GUT	GUTTER
HWU	HOT WATER UNIT
HYB	HYBRID FLOOR
L	LINEN
MR	METAL ROOF
MW	MICROWAVE OVEN
NGL	NATURAL GROUND LEVEL
OBS	OBSCURED GLASS
P	PANTRY
R	ROBE
RL	REDUCED LEVEL
RWH	RAIN WATER HEAD
RWT	RAIN WATER TANK
S	STORAGE
TOW	TOP OF WALL
TL	TIMBER LAMINATE
WC	WATER CLOSET
WM	WASHING MACHINE
SD	SMOKE DETECTOR

Sheet List

Sheet No.	Sheet Name	Drawn By	Current Revision Date	Revision
CC.01	COVER SHEET	ROHIT	21-10-2026	
CC.02A	GENERAL NOTES	ROHIT	15-05-2026	
CC.03	LOCATION PLAN AND SITE PLAN	ROHIT	21-10-2026	
CC.04	SITE ANALYSIS AND SEDIMENT CONTROL	ROHIT	15-05-2026	
CC.05	GROUND FLOOR PLAN	ROHIT	21-10-2026	
CC.07	ROOF PLAN	ROHIT	21-10-2026	
CC.08	ELEVATION 01	ROHIT	21-10-2026	

Sheet List

Sheet No.	Sheet Name	Drawn By	Current Revision Date	Revision
CC.09	WINDOW & DOOR SHEDULE	ROHIT	21-10-2026	
CC.10	SECTIONS	ROHIT	15-05-2026	
CC.11	FLOOR AREA PLAN	ROHIT	15-05-2026	
CC.12	RENTABLE AREA PLAN	ROHIT	15-05-2026	
CC.14	COLOR SCHEDULE	ROHIT	15-05-2026	
CC.15	LANDSCAPE PLAN	ROHIT	15-05-2026	
CC.02B	GENERAL NOTES	ROHIT	5-05-2026	CC ISSUE

CDC ISSUE

2R DESIGN STUDIO
Email: rohit@2rdesign.com.au
Ph. 0451117566
BUILDING DESIGNERS ASSOCIATION OF AUSTRALIA

COPY RIGHT THIS DRAWING IS THE PROPERTY OF 2R DESIGN STUDIO AND MAY NOT BE RETAINED,COPIED IN WHOLE OR IN PART OR USED OTHER THAN FOR THE SPECIFIC USE LICENSED AND ISSUED WITHOUT THE WRITTEN CONSENT.

REV	DATE	DESCRIPTION	BY
3	21-10-2026	FOR CONSTRUCTION	
2	15-05-2026	CC ISSUE PCA	
1	5-05-2026	CC ISSUE	

PROJECT:
LOT 53 4 KILEEN STREET
4 KILLEEN STREET AUBURN NSW 2144

DRAWING TITLE:
COVER SHEET

NORTH:

LOT NO: 53 DP :
DATE: 3-05-2026
DRAWN BY: ROHIT
CHECKED BY: 2R DESIGN

SCALE: 1 : 100

DRAWING No: CC.01


REV: 3

ISSUED BY:

CLIENT NAME
DEPENDRA ACHARYA


SIGN

A3

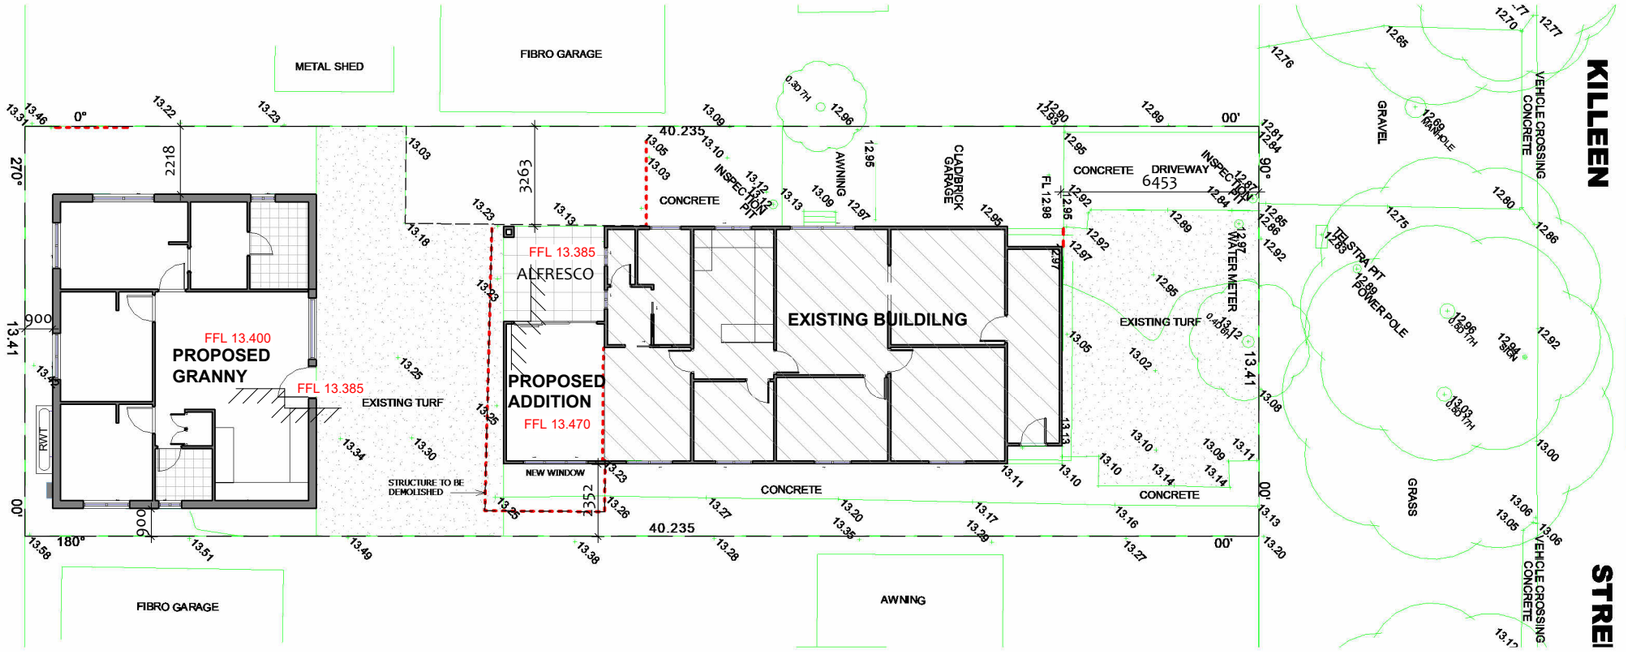

1 CC - LOCATION AND SITE PLAN

1 : 200

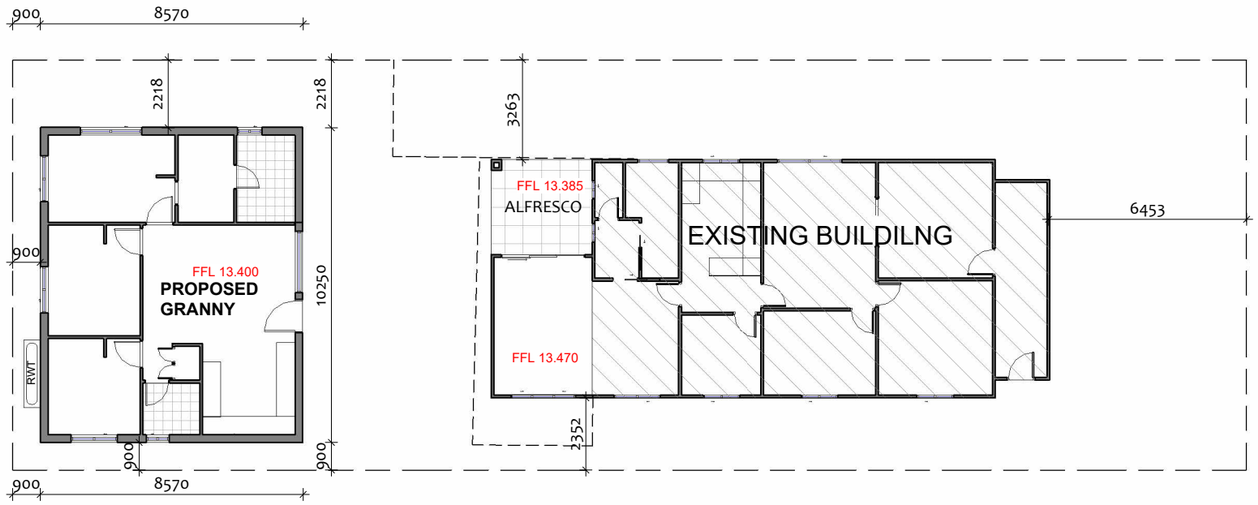

2 CC - LOCATION AND SITE PLAN SETBACK

1 : 200

CDC ISSUE

REV	DATE	DESCRIPTION	BY
3	21-10-2026	FOR CONSTRUCTION	
2	15-05-2026	CC ISSUE PCA	
1	5-05-2026	CC ISSUE	

2R DESIGN STUDIO
Email: rohit@2rdesign.com.au
Ph. 0451117566
BUILDING DESIGNERS ASSOCIATION OF AUSTRALIA

COPY RIGHT THIS DRAWING IS THE PROPERTY OF 2R DESIGN STUDIO AND MAY NOT BE RETAINED,COPIED IN WHOLE OR IN PART OR USED OTHER THAN FOR THE SPECIFIC USE,LICENSED AND ISSUED WITHOUT THE WRITTEN CONSENT

PROJECT:

LOT 53 4 KILEEN STREET

4 KILLEEN STREET AUBURN NSW 2144

DRAWING TITLE:

LOCATION PLAN AND SITE PLAN

NORTH:


LOT NO: 53	DP :	SCALE: 1 : 200	DRAWING No: CC.03
DATE: 3-05-2026			REV: 3
DRAWN BY: ROHIT			ISSUED BY:
CHECKED BY: 2R DESIGN			

CLIENT NAME: DEPENDRA ACHARYA


SIGN

A3

IMPORTANT NOTES:
ALL DIMENSIONS AND NOTES ON ALL PLANS MUST BE CHECKED AND VERIFIED BY BUILDERS AND OWNER PRIOR TO COMMENCEMENT OF ANY BUILDING WORKS. TO CLARIFY AND CONFIRM WITH CONSTRUCTION COMPANY FOR DISCREPANCIES ON ALL DOCUMENTS AND PLANS PROVIDED FOR CONSTRUCTION.ANY WORK INDICATED ON THE PLAN BUT NOT IN THE SPECIFICATION BUT WHICH IS NECESSARY AS PART OF THE CONTRACT,VARIATION TO PLANS,SPECIFICATIONS MAY NOT BE MADE WITHOUT THE WRITTEN CONSENT OF OWNER.IT IS THE RESPONSIBILITY OF THE BUILDER/END USER TO VERIFY PLANS AND SPECIFICATIONS AS TO THEIR ACCURACY AND COMPLY CURRENT BCA AND AUSTRALIAN STANDARDS.
WINDOWS TO COMPLY WITH 3.9.3.5 OF THE BCA.

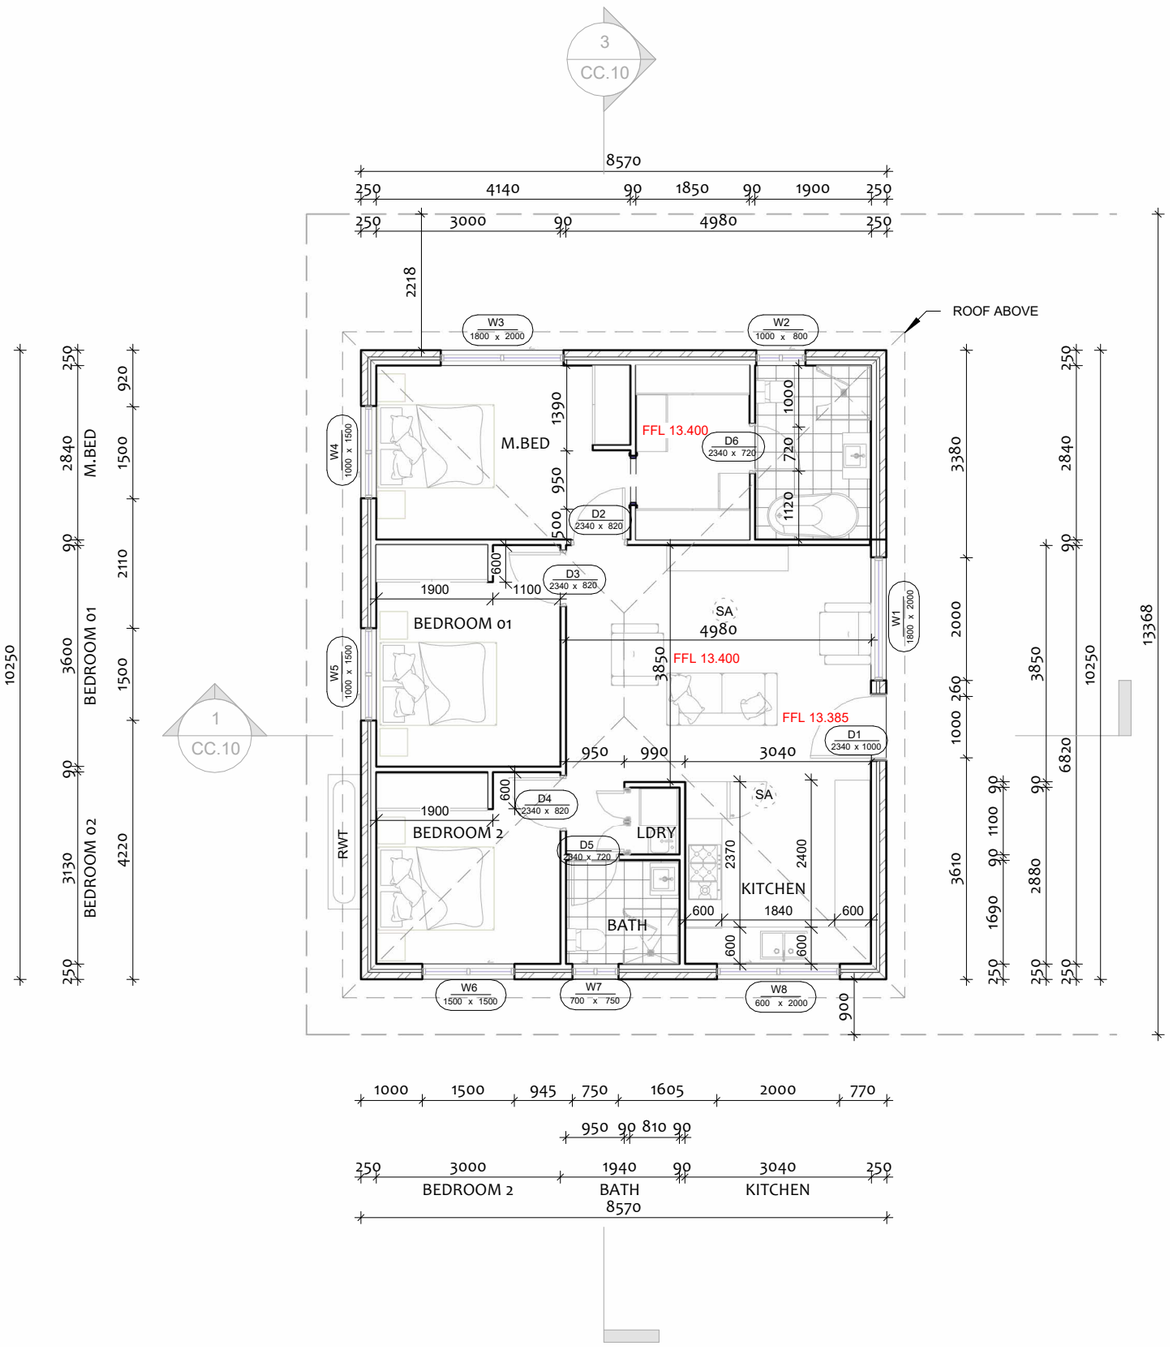

1 GROUND FLOOR PLAN
1 : 100

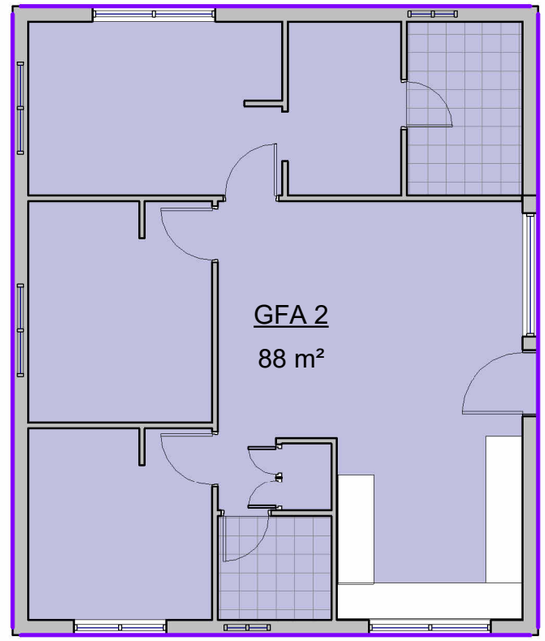

2 Ground Floor
1 : 100

Area Schedule (Gross Building)	
Name	Area
Ground Floor	
GFA 2	88 m²
Ground Floor: 1	88 m²
Grand total: 1	88 m²

CDC ISSUE

2R DESIGN STUDIO
Email: rohit@2rdesign.com.au
Ph. 0451117566
BUILDING DESIGNERS ASSOCIATION OF AUSTRALIA

COPY RIGHT THIS DRAWING IS THE PROPERTY OF 2R DESIGN STUDIO AND MAY NOT BE RETAINED,COPIED IN WHOLE OR IN PART OR USED OTHER THAN FOR THE SPECIFIC USE,LICENSED AND ISSUED WITHOUT THE WRITTEN CONSENT.

REV	DATE	DESCRIPTION	BY
3	21-10-2026	FOR CONSTRUCTION	
2	15-05-2026	CC ISSUE PCA	
1	5-05-2026	CC ISSUE	

PROJECT:
LOT 53 4 KILEEN STREET
4 KILLEEN STREET AUBURN NSW 2144

DRAWING TITLE:
GROUND FLOOR PLAN

NORTH:

LOT NO: 53 DP :
DATE: 3-05-2026
DRAWN BY: ROHIT
CHECKED BY: 2R DESIGN

SCALE: 1 : 100

DRAWING No: **CC.05**


REV: 3

ISSUED BY:

CLIENT NAME: DEPENDRA ACHARYA
SIGN

A3

IMPORTANT NOTES:
ALL DIMENSIONS AND NOTES ON ALL PLANS MUST BE CHECKED AND VERIFIED BY BUILDERS AND OWNER PRIOR TO COMMENCEMENT OF ANY BUILDING WORKS. TO CLARIFY AND CONFIRM WITH CONSTRUCTION COMPANY FOR DISCREPANCIES ON ALL DOCUMENTS AND PLANS PROVIDED FOR CONSTRUCTION.ANY WORK INDICATED ON THE PLAN BUT NOT IN THE SPECIFICATION BUT WHICH IS NECESSARY AS PART OF THE CONTRACT,VARIATION TO PLANS,SPECIFICATIONS MAY NOT BE MADE WITHOUT THE WRITTEN CONSENT OF OWNER.IT IS THE RESPONSIBILITY OF THE BUILDER/END USER TO VERIFY PLANS AND SPECIFICATIONS AS TO THEIR ACCURACY AND COMPLY CURRENT BCA AND AUSTRALIAN STANDARDS.
WINDOWS TO COMPLY WITH 3.9.3.5 OF THE BCA.

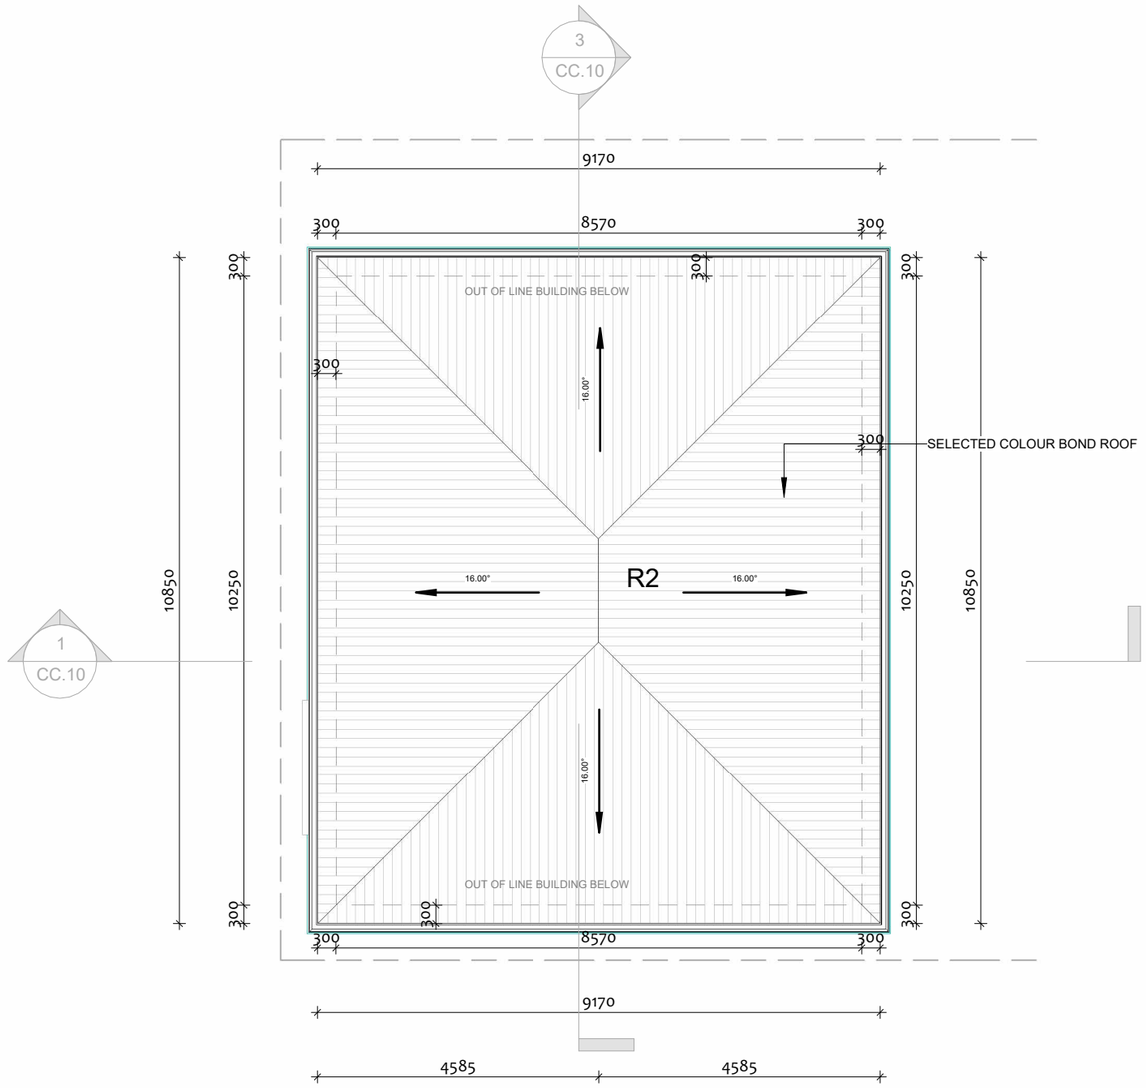

1 ROOF PLAN
1 : 100

Roof Schedule			
Mark	Base Level	Area	Comments
R2	GRANNY FLAT CL.	104 m²	Colorbond Roof

CDC ISSUE

2R DESIGN — STUDIO —
Email: rohit@2rdesign.com.au
Ph. 0451117566
BUILDING DESIGNERS ASSOCIATION OF AUSTRALIA

COPY RIGHT THIS DRAWING IS THE PROPERTY OF 2R DESIGN STUDIO AND MAY NOT BE RETAINED,COPIED IN WHOLE OR IN PART OR USED OTHER THAN FOR THE SPECIFIC USE,LICENSED AND ISSUED WITHOUT THE WRITTEN CONSENT.

REV	DATE	DESCRIPTION	BY
3	21-10-2026	FOR CONSTRUCTION	
2	15-05-2026	CC ISSUE PCA	
1	5-05-2026	CC ISSUE	

PROJECT:
LOT 53 4 KILEEN STREET
4 KILLEEN STREET AUBURN NSW 2144

DRAWING TITLE:
ROOF PLAN

NORTH:

LOT NO: 53 DP :
DATE: 3-05-2026
DRAWN BY: ROHIT
CHECKED BY: 2R DESIGN

SCALE: 1 : 100

DRAWING No: CC.07

REV: 3

ISSUED BY:

CLIENT NAME
DEPENDRA ACHARYA


SIGN

A3




1 North Elevation

1 : 100

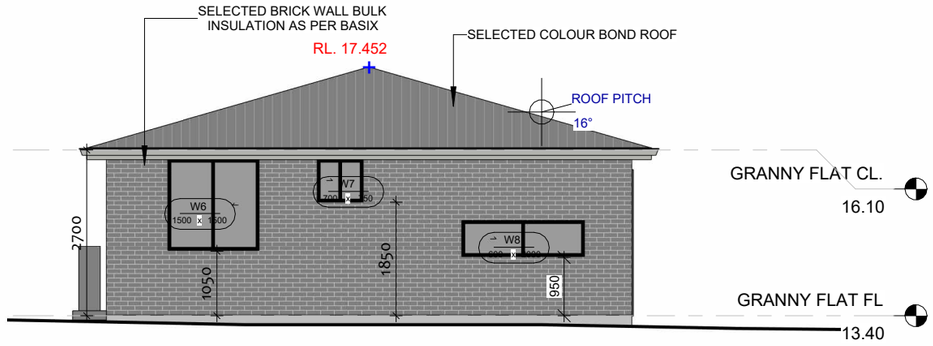


3 East Elevation

1 : 100

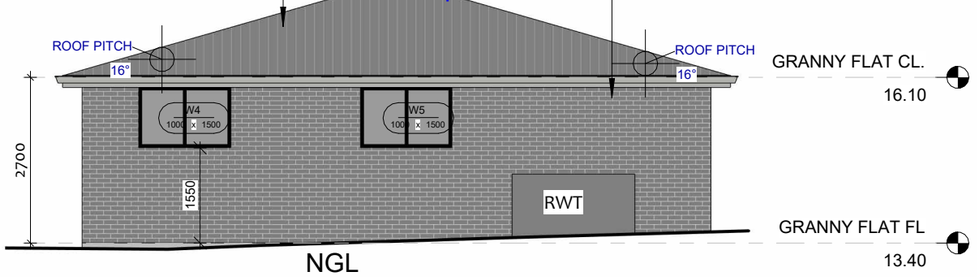

2 South Elevation

1 : 100

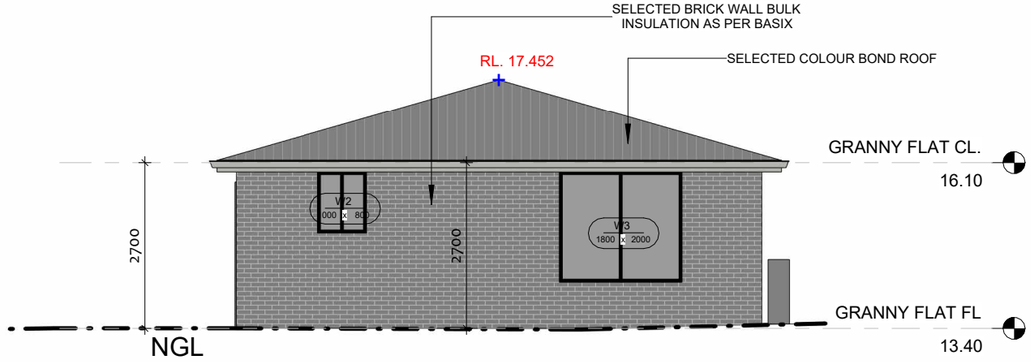

4 West Elevation

1 : 100

CDC ISSUE

2R DESIGN STUDIO

Email:
rohit@2rdesign.com.au
Ph. 0451117566

COPY RIGHT THIS DRAWING IS THE PROPERTY OF 2R DESIGN STUDIO AND MAY NOT BE RETAINED,COPIED IN WHOLE OR IN PART OR USED OTHER THAN FOR THE SPECIFIC USE,LICENSED AND ISSUED WITHOUT THE WRITTEN CONSENT.

REV	DATE	DESCRIPTION	BY
3	21-10-2026	FOR CONSTRUCTION	
2	15-05-2026	CC ISSUE PCA	
1	5-05-2026	CC ISSUE	

PROJECT:

LOT 53 4 KILEEN STREET

4 KILLEEN STREET AUBURN NSW 2144

DRAWING TITLE:

ELEVATION 01

NORTH:

LOT NO: 53 DP :

DATE: 3-05-2026

DRAWN BY: ROHIT

CHECKED BY: 2R DESIGN

SCALE: 1 : 100

DRAWING No: CC.08

RE V-3

ISSUED BY:

CLIENT NAME: DEPENDRA ACHARYA

SIGN

A3

Window Schedule 1					
Mark	Height	Width	Sill Height	Head Height	Description
GRANNY FLAT FL					
W1	1800	2000	600	2400	FIXED with AWNING
W2	1000	800	1550	2550	SLIDING
W3	1800	2000	750	2550	SLIDING
W4	1000	1500	1550	2550	SLIDING
W5	1000	1500	1550	2550	SLIDING
W6	1500	1500	1050	2550	SLIDING
W7	700	750	1850	2550	SLIDING
W8	600	2000	950	1550	SLIDING
GRANNY FLAT FL: 8					

Door Schedule 1				
Mark	Height	Width	Count	Description
Ground Floor				
D1	2340	1000	1	TIMBER DOOR
D4	2340	820	1	SOLID FLUSH DOOR
D3	2340	820	1	SOLID FLUSH DOOR
D7	2300	2650	1	SLIDING DOOR
D2	2340	820	1	SOLID FLUSH DOOR
D5	2340	720	1	SOLID FLUSH DOOR
D6	2340	720	1	SOLID FLUSH DOOR
Ground Floor: 7				

CDC ISSUE

2R DESIGN STUDIO

Email:
rohit@2rdesign.com.au
Ph. 0451117566

COPY RIGHT: THIS DRAWING IS THE PROPERTY OF 2R DESIGN STUDIO AND MAY NOT BE RETAINED,COPIED IN WHOLE OR IN PART OR USED OTHER THAN FOR THE SPECIFIC USE,LICENSED AND ISSUED WITHOUT THE WRITTEN CONSENT.

REV	DATE	DESCRIPTION	BY
3	21-10-2026	FOR CONSTRUCTION	
2	15-05-2026	CC ISSUE PCA	
1	5-05-2026	CC ISSUE	

PROJECT:

LOT 53 4 KILEEN STREET

4 KILLEEN STREET AUBURN NSW 2144

DRAWING TITLE:

WINDOW & DOOR SHEDULE

NORTH:

LOT NO: 53 DP .

DATE: 3-05-2026

DRAWN BY: ROHIT

CHECKED BY: 2R DESIGN

SCALE:

DRAWING No: CC.09

REV: 3

ISSUED BY:

CLIENT NAME

DEPENDRA ACHARYA

SIGN

A3