


Sheet List	
Sheet Name	Sheet Number
PROPOSED GROUND FLOOR PLAN	07/28
PROPOSED FIRST FLOOR PLAN	08/28
BUILDING ELEVATIONS 1	10/28
CROSS SECTIONS + BASIX DETAILS	12/28
COLOURS AND FINISHES	20/28
PROPOSED ROOF PLAN	09/28
EROSION AND SEDIMENT CONTROL	25/28
NOTES AND SPECIFICATIONS	01/28
PROPOSED DEMOLITION PLAN	26/28
BUILDING ELEVATIONS 2	11/28
PROPOSED DRIVEWAY	17/28
PROPOSED SITE PLAN	02/28
PROPOSED BASEMENT PLAN	06/28
POOL PLANS 1	13/28
COVER SHEET	00
POOL PLANS 2	14/28
3D PERSPECTIVE 1	21/28
DWELLING 1 WINDOW & DOOR SCHEDULE	27/28
DWELLING 2 WINDOW & DOOR SCHEDULE	28/28

ISSUED FOR COMPLYING DEVELOPMENT APPLICATION

PROPOSED DEVELOPMENT
26 LUCINDA AVE, BASS HILL

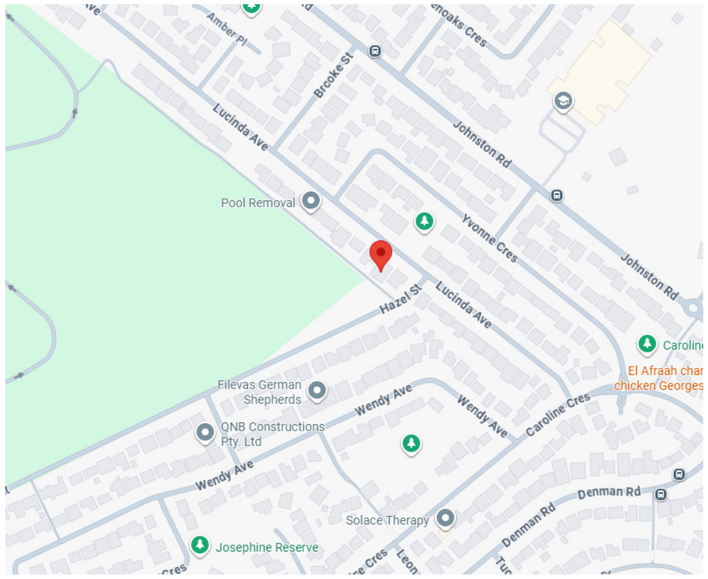

SITE LOCATION MAP

26 LUCINDA AVE, BASS HILL

CEDAR DESIGNS

IBRAHIM MUSTAPHA
BDAA ACCREDITED - 6450
BDAA MEMBER - 2360 - 17
REGISTERED DESIGN PRACTITIONER - DEP0000079

CEDAR DESIGNS PTY LTD
EMAIL: INFO@CEDARDESIGNS.COM.AU
WEBSITE: WWW.CEDARDESIGNS.COM.AU
PHONE: +61 410 289 126

ISSUE	DESCRIPTION
A	ISSUED FOR CLIENT REVIEW

Scale: @ A2

COVER SHEET

00

GENERAL NOTES
- Do not scale drawings, use figured dimensions only.
- All dimensions and levels are to be verified on site before any work commences.
- All work is to be carried out in accordance with the AS and NCC standards.

COPYRIGHT:
This document is COPYRIGHT and the property of CEDAR DESIGNS PTY LTD. It is not to be retained, copied or used without the prior written permission of CEDAR DESIGNS PTY LTD.

17/08/2026 5:20:37 PM

PRELIMINARY NOTES & SPECIFICATIONS

GENERAL NOTES

1. All works shall be completed in accordance with the architectural plans prepared by Cedar Designs Pty Ltd
2. All works shall be completed in accordance with the Stormwater Drainage plans prepared by the project engineer
3. All works shall be completed in accordance with the structural plans prepared by the project engineer
4. All works shall be completed in accordance with all the relevant Australian standards and the NCC
5. All works shall be completed in accordance with the Basix Certificate relevant to the project.
6. All works shall be completed in accordance with any relevant DA, CDC or CC conditions.
7. All dimensions shall be verified on site.
8. Do not scale the drawings, use figured dimensions only.
9. A copy of the Architectural Plans must remain on site at all times during construction.
10. Any discrepancies must be reported to Cedar Designs Pty Lyd for revisions before any work commences.
11. Cedar Designs Pty Ltd will not be responsible for any modifications made on site unless modifications were made and approved on the plans prior to the work commencing.

GENERAL CONDITIONS

1. The Contractor is to nominate the earliest starting time for commencement of work on site, and the expected time of completion.
2. The lowest tender price may not necessarily be given the contract.
3. The contract shall be Lump Sum Fixed Price, no rise and fall allowed. Two copies of the contract are to be signed prior to commencement of work on site.
4. The contract sum shall be inclusive of GST.
5. The conditions and clauses of this document will form part of the Contract.
6. All relevant SAA codes referred to in the specifications and the Architectural and Engineering drawings, and all the by-laws, regulations and ordinances of all the authorities having jurisdiction over the works shall be adhered to.
7. The Contractor shall provide all materials, labour, plant, equipment, tools and everything else necessary and shall carry out and complete the whole of the works in an expeditious, safe and workmanlike manner.
8. The Contractor shall be responsible for the safety of all the workers, the surrounding Proprietors and invited visitors, during construction and ensure that all work is undertaken in accordance with the latest Work Cover rules and regulations.
9. The Contractor shall be responsible for the whole of the work including that of the sub-Contractors and for any matter arising therefrom and shall indemnify the Proprietor, his invitees and his agents against all claims, demands and actions, costs, loss, damage or expense in relation to the same.

PRELIMINARIES

1. Check all dimensions and set outs on site and communicate any discrepancies to the Architect for verification and approval of revisions BEFORE work commences. Extras arising out of the Contractor's or Sub-Contractor's non-adherence to the above shall NOT be allowed.
2. All necessary insurances (ie works, workers' compensation, public liability etc) shall be taken out by the Contractor and policy numbers or receipts issued to the Proprietor. This application has been lodged with Council and duly approved. The Proprietor will pay for all other Council fees and the Home Owner's insurance.
3. The Contractor shall allow for and pay all Statutory Authority fees in connection with the works, arrange for all the necessary inspections and obtain all permits.
4. The Contractor must provide new materials, and workmanship of the best quality throughout to the satisfaction of the Proprietor and unless otherwise specified in accordance with the requirements of the relevant codes and statutory authorities.

WORK, HEALTH AND SAFETY

Workplaces: Regulations of the Work Health & Safety Act as applicable in the State in which the building work is to proceed are to be complied with.
Under the Act if a structure is to be used as, or at a workplace it must be designed to be without risk to health and safety by including testing and analysis, addressing the suitability of the design for the ultimate use of the structure as well as materials, method of construction, maintenance and future demolition. The builder is to comply with the regulations of the Work Health and Safety Act 2011 for all construction on site. If the structure will be used as or at a workplace, a Safety Report is to accompany plans and specifications and be distributed to the Builder, Certifier or Council and the Client.

BEFORE BUILDING BEGINS + OTHER CONDITIONS

1. Provide temporary security fencing around the site and attach all the necessary Safety Signs and the Contractor's contact details as required by the Council.
2. Keep site clear of all rubbish and debris during construction.
3. Street, and footpaths to be kept safe and clean at all times.
4. If for any reason you are required to block the footpath, you are required to safely escort all pedestrians
5. Services such as gas must be checked and discontinued from the site prior to the commencement of works.

EXCAVATION

1. Provide and maintain sediment controls around the site at all times, as required by Council.
2. Excavate the site and leave ready for constructing footings for walls, columns, piers and other structural components as per the Engineer's drawing and specifications.
3. Excavate to achieve the areas, levels and heights as shown on the Architectural drawings.
4. Excavate for all necessary service and drain lines, including stormwater and sub-surface water.
5. Protect and support all services, property and structures adjacent to excavations (including neighbouring properties and footpaths) until making good is completed.
6. Throughout construction keep excavated, levelled and filled areas free of water. Immediately before placing concrete or masonry on ground remove all water and foreign matter. Prevent water flow over freshly laid work.
7. Remove all unwanted excavated material from site, and keep site clear during construction.
8. Unless otherwise noted by the developer excavation cost is assumed there is no rock, where rock is encountered additional charges may apply.

TERMITE TREATMENT

Allow for the provision of Termi mesh (or other approved) termite prevention to the whole of the house as required in the BCA and in accordance with the requirements of AS3660.1 - 1995. Provide a certificate from an accredited installer.

CONCRETE

1. The Concreter is to use the Engineer's drawings and specifications for the sizing of all reinforced concrete components, including footings, slabs, reinforced concrete block work, stairs/steps, paths etc.
2. Allow for the supply and installation of formwork, steel reinforcement, bedding material, waterproof membranes, expansion joints and slip joints.
3. Concrete strength and slump as per Engineer's specification.
4. Driveway finish shall be in accordance with the detailed provided on the Architectural plans.
5. Any discrepancies with the structural specifications should be reported to the project engineer.

BRICKWORK

1. Allow for all the brickwork shown on the architectural drawings, including all walls and columns.
2. Allow for brick-on-edge window sills and header courses on top of both the deck balustrades.
3. All internal and external bricks to be ready for render unless noted otherwise.
4. All bricks shall be accurately bonded and carried up true and plumb in level courses to the heights and thicknesses shown on the drawings.
5. Set out shall be seven courses, and seven joints in height shall equal 600mm
6. Provide all brick ties (in stainless steel) and the like, including damp-proof courses and flashing's (in super alcor), weepholes and brick on edge details.

RENDER

1. All internal and external brickwork to be cement rendered except the, feature walls, which should be made ready for tiling with stone tiles, and others for Alucobond or cladding further details will be provided. The walls to be rendered to be made ready for painting, except for wet area walls, which shall have a steel trowel finish, ready for tiles.
2. Allow for cement rendered finish to the soffit of both the upper floor concrete slab decks and the soffit of the Entry Porch roof.
3. All finishes must be in accordance with the Architectural Plans

GARAGE DOOR

1. Provide a garage door panel lift door for the Garage and install it and a remote controlled automatic door opening system. Provide three remote controls.
2. The panel design for the garage door shall be as shown on elevations.
3. Selected Garage door finish to be as per Architectural Specifications and finished as per the architectural plans.

METAL

1. All steel angles / lintels and fixings are to be sized and installed as per the Engineer's details and specifications. All to be hot-dipped galvanised.
2. Install box gutters and down pipes to the whole of the house, including the Entry Porch roof, in accordance with the Engineer's drawings and specifications
3. Use the Stormwater Layout drawing to determine the location of the downpipes.
4. Prior to completion of works the contractor shall issue a certificate of compliance for the works completed.

TIMBER

1. All timber to be new, straight, well-seasoned and free from defects. Provide all necessary templates, linings, blocks, stops, ironwork, ironmongery, nails, screws, bolts, plugs and fixings generally.
2. All structural timbers shall be min. F7 stress grade. All timbers shall be sized and installed in accordance with SAA TIMBER FRAMING CODE - AS1684-1992.
3. Any timber member required but not shown on drawings or specified shall be sized and installed to AS1684.
4. The fabricator of the roof frame shall provide a certificate of structural adequacy.

FRONT DOOR

1. Provide a front door, either timber or similar as per the details of the architectural plans.
2. Front door finish to be as specified on the architectural plans.
3. All structural timbers shall be min. F7 stress grade. All timbers shall be sized and installed in accordance with SAA TIMBER FRAMING CODE - AS1684-1992.

TIMBER FLOORING

1. Allow for the installation of new solid **Select** quality secret nailed hardwood tongue & groove flooring for the stairs, all the first floor, except wet areas which shall be prepared for tiling.
2. Allow a prime cost sum of **$100 per square meter** supplied for the timber flooring. The exact species will be chosen later by the owners or developer.
3. The flooring to be sanded and polished with two coats of Synteko URETHANE

TIMBER LINING TO CONCRETE STAIRS

1. Fix timber stair treads and rises in the same timber as the floor. The treads are to have a bull nose edge that cantilevers at least 25mm past the riser.
2. The treads and rises are to be sanded and polished as per the floor finish.

INTERNAL HANDRAIL & BALUSTRADE

1. Install a toughened **glass** balustrade along one side of the stairs and around the Foyer void with 50mm dia stainless steel posts and a
2. The top of the handrail is to be fixed a minimum of 900mm above the nosing of the stairs and 1000mm above the Upper Floor hallway floor level.
3. All Railings shall be installed as per the Australian Standards.
4. A certificate must be issued by the installer at the completion of works.

KITCHEN

1. The Proprietor may nominate a sub-contractor for the fabrication and installation of the kitchen cupboards and benchtops.
2. The Contractor is to provide all the required services (electrical, gas, water, sewage (etc) as shown on the detail drawings, to allow for the connection of all the kitchen appliances.
3. The Contractor is to allow the kitchen fabricator access to the site to measure up and install the kitchen.
4. Allow a **Provisional Sum of $20,000** for the kitchen cupboards, bench top and splashback, all of which will be designed and chosen later by the owners or developers.
5. Unless any prior agreement is made, the the proprietors will supply the kitchen appliances.

BEDROOM BUILT-IN & WIR CUPBOARDS

1. The Proprietor will nominate a sub-contractor for the fabrication and installation of the bedroom built-in and WIR cupboards.
2. The Contractor is to install a bulkhead with surrounding cornice set out from the walls where the built-ins will be installed. Details will be issued at a later date.
3. Allow a **Provisional Sum of $7,000** for built-ins and WIR, all of which will be designed later.

LAUNDRY CUPBOARDS, CHUTE, TOWEL SHELVES & LINEN CUPBOARD

1. The Proprietor will nominate a sub-contractor for the fabrication and installation of the laundry cupboards, chute and linen press.
2. The Contractor is to provide all the required services as shown on the detail drawings, to allow the connection of the laundry appliances.
3. Allow a **Provisional Sum of $5,000** for the laundry cupboards, chute, towel shelves and linen cupboard, all of which will be designed later.

BATHROOM AND ENSUITE VANITIES

1. The Proprietor will nominate a sub-contractor for the fabrication and installation of the Bathroom and Ensuite vanity units, which will have polyurethane cupboards and granite bench tops.
2. The Contractor is to provide all the required services as shown on the detail drawings, to allow the connection of the vanity fixtures and services.
3. Allow a **Provisional Sum of $15,000** for the Bathroom and Ensuite vanity units, all of which will be designed later.
4. The proprietors will supply the vanity basins.

INTERNAL DOORS

Install solid **flush** doors, ready for painting, to all internal door openings. Fix all door furniture as required.

SKIRTINGS

Install 100x25 Splayed **Red Cedar** timber skirting's to all first floor rooms/areas except for wet areas, all ground floor skirting's shall be tiled matching with the selected floor tiles to be nominated at a later date.

ARCHITRAVES

Install %75x25 Splayed profiled timber architraves around all doors that have timber jambs in either finger-jointed pine or maple, ready for painting.

SUSPENDED CEILING

1. Provide a suspended flush plasterboard lined ceiling throughout the whole the Ground Floor and first floor to allow for recessed down lights. The ceiling is to finish just below the soffit of the concrete beam between the Kitchen and Dining Room.
2. Allow for 20 linear metres of bulkheads to the Ground Floor and first floor level to incorporate air conditioning ducts as required. The exact layout for the bulkheads will be determined in consultation with the air conditioning sub-contractor.
3. Provide a suspended ceiling in the Laundry and Ground Floor Bathroom as required to conceal the Upper Floor plumbing.

PLASTERBOARD

1. Install plasterboard to all ceilings.
2. Plasterboard for ceilings shall be 13mm thick, flush jointed taped and set. All nail holes to be filled and joints sanded smooth ready for painting.
3. All Plasterboard works shall be in accordance with the Australian Standards, a certificate of compliance should be issued by the selected contractor.

SHADOW MOULDS & CORNERS

1. Install **shadow moulds** to all Ground Floor and Upper Floor wall and ceiling junctions, including in the Bathrooms and Laundry, which are to be fitted between the tiles and the ceiling.
2. All shadow moulds and corners are to be in plastic.

FIBRE CEMENT

1. Provide 6mm thick fibre cement lining, equal to "J Hardies" for the front Upper Floor Balcony, entry patio and rear ground floor Deck ceilings.
2. Fibre cement Joints for ceilings are to be waterproof taped and set flush.
3. All fibre cement is to be prepared for painting.

ALUMINIUM WINDOWS & DOORS

1. Install Aluminium windows and external doors THROUGHOUT fabricated from **anodised Aluminium** as per the Door and Window Schedule.
2. The Contractor is to install **door stops** to all internal doors and **catches** to all external doors. These will be supplied by the Proprietor.
3. The Aluminium doors and windows shall be installed in accordance with the Australian Standards and the Basix Certificate applicable to this project.
4. The Contractor must issue a certificate of compliance at the completion of works.

AIR CONDITIONING

Allow a **Provisional Sum of $25,000** for the supply and installation of a reverse cycle, ducted air conditioning system, the layout of which will be determined later.

PLUMBING + WATERPROFFING

1. Connect all plumbing lines and fittings shown on the drawing in accordance with Water Board regulations and requirements and obtain a Certificate of satisfactory completion.
2. Provide a Rinnai 36 instantaneous gas Hot Water System in a Rinnai supplied recessed metal cabinet. The HWS is to be located between the Laundry door and the Kitchen window.
3. Extend the hot and cold water supply to all the fittings shown in the architectural and detail drawings. Hot water pipes to be insulated.
4. Provide three new external hose cocks. One to be fitted to the rainwater tank outside the Garage, one at the front yard, and one at the rear of the house before the rear Patio.
5. Waterproof the whole of all the Bathroom floors, walls and baths surrounds and all shower recesses as per *AS3740-1994 Waterproofing of Wet Areas within Residential buildings*.
6. The Upper Floor Balcony's, ground floor rear Patio and the Entry Porch roof are to be waterproofed with an approved membrane and obtain a guarantee of 7 years minimum, before the installation of the balustrade.
7. The contractors must issue a certificate of compliance at the completion of works.

GAS SERVICE

1. Provide a new gas service in accordance with AGL regulations and requirements and obtain a Certificate of satisfactory completion. The meter is to be located behind the front fence in the bottom right hand corner of the site.
2. Provide the following gas connections; hot water system, hot plates in the kitchen, two bayonet space heater connections at the ground floor, and one external barbeque connection on rear patio.

RAINWATER TANK

1. Connect one of the downpipes to the rainwater tank outside as per the architectural plans and stormwater plans.
2. The rain water tank size must be as per the basix certificate.
3. Connect one external hose cock to the rainwater tank.
4. The rainwater tank will be supplied by the Proprietor.

STORMWATER

1. Use the Engineer's **Stormwater Details** Plan for the sizing of the stainless steel box gutter and the location and sizing of the downpipes, grated drains and pits.
2. All Stormwater works must be completed as per the Stormwater Plans and councils DCP.
3. Any misunderstanding or discrepancies in the stormwater plans must be reported to the engineers.
4. A certificate of compliance must be issued at the completion of works.
5. The developer must check any relevant conditions within the approved documentation for any additional requirements such as easement registration or positive covenants or anything similar.

CAR PARKING:

1. All car Parking shall be in Accordance with the Architectural Plans and comply with the provisions of the local council or SEPP.
2. All car parking and loading bays to be kerbed, guttered, sealed, drained, line marker and landscaped.
3. Drainage of surface water into neighbouring propertied is Strictly Prohibited unless an easement is obtained.
4. Prior to any works on councils assetts for the purpose of the construction of a driveway, a work permit, or driveway design shall be obtained from the relevant local council.

ELECTRICAL, TELEPHONE & TELEVISION

1. All work to be carried out in accordance with the supply authority's requirements and the SAA Wiring Rules.
2. The electrician is to install a galvanised pole at the front of the property in the location shown on the Electrical Layout, to allow for the electrical mains connection and for pay tv connection from the pole in the street. The main lines are to be connected to the metre box underground. The meter box is to be installed one the side before the garage window. The circuit board is to be fixed in the garage.
3. The electrician is to allow for the complete wiring of the house, and for the connection of all the lights, GPOs, telephone, free-to-air television, pay television lines, broadband connection and all other fixtures as specified and/or as shown on the Electrical Layout.
4. The electrician is to allow for a separate power circuit to the Kitchen and another circuit for the Family Room to allow for power sharing over the rest of the circuits.
5. The electrician is to allow for the installation of two safety switches on the electrical mains board. One for the Kitchen and one for the remaining circuits.
6. At the completion of works the contractor must issue a certificate of compliance for the completed works.

SECURITY SYSTEM

Allow a **provisional sum of $3,000** for the supply and installation of an infra red security system. The layout and design will be determined later.

WALL & FLOOR TILING

1. The Contractor is to allow the following Prime Cost Sums for tiles: Floor tiles - $50 per square metre supplied Wall tiles - $45 per square metre supplied.
2. Allow for floor tiles to **all external door thresholds**, The entire ground floor the Entry Porch and step, the rear Patio, the Upper Floor Bathrooms and Ensuite, the Upper Floor balcony and, and ground floor patio.
3. The grouting for all the floor tiles is to be neutral in colour and to finish flush with the top of the tiles.
4. Allow for wall tiles on all walls (and bath/spa surround) from floor to ceiling for all Bathrooms and the Laundry.
5. For the Laundry allow for wall tiles from the benches to the underside of the overhead cupboards.
6. The tiles will be chosen by the Proprietor at a later date.
7. Larger scale detail drawings for all wet areas will be supplied at a later date.

PAVING AND LANDSCAPING WORKS.

1. The Contractor is to allow a **Prime Cost Sum of $50** per square metre for pavers, which will be selected later.
2. Install pavers to both side passageways leading from the front of the Garage and the front of the entry Porch to the back of the rear Patio.
3. Pavers are to be laid on a firm sand bed over compacted road base. Pavers are to have no gap between them, and all joints to be filled with sand. All exposed edge pavers to be bedded in 75mm thick concrete base.
4. Install pavers to the drive way, with a 50mm gap between each paver to fill with either grass or white pebbles, this will be decided at a later date.
5. All Landscape works shall be completed as per the Landscape plans inclusive of all plans and trees as specified.
6. The Contractor is not required to price any other landscaping works unless any other agreement has been made prior to works.
7. At the completion of Landscape works the developer is required to contact Cedar Designs Pty Ltd or the Project Landscape architect for a inspection of the completed works.
8. A Certificate of completion is required to be issued.

TREE REMOVAL WORKS AND TREE PROTECTION WORKS

1. In most cases, trees are protected in NSW and must not be removed unless an approval for tree removal has been granted by Council
2. Tree removal must be in accordance with the Approved plans, and DA Conditions, or separate tree removal permit obtained from Council.
3. All trees on site which are not approved for removal must be retained and protected during construction under the direction of an arborists.
4. All trees on public land must be retained and protected under the direction of an arborists unless their removal has been approved by Council.
5. Fines apply for the removal or damage of protected trees.
6. Cedar Designs Pty Ltd shall not be responsible for any trees removed without approval, this shall be the full responsibity of the developers.

INSULATION

Install aluminium faced sarking under all tiled roofs, and R3 fibre glass insulation above all ceilings in the house.
A certificate must be provided by the installer.

MIRRORS

1. Install mirrors to all Bathrooms and the Ensuite, over the vanity units. Mirrors to be 1000 high with revelled edges and extend for the full length of the vanity benches unless any other agreement has been made prior to works.
2. All mirrors to have all edges sealed and waterproofed against moisture penetration and be **surface mounted** to Proprietor's instructions.

FITTINGS / PC ITEMS

1. All hinges, keyed winders, and the like are to be supplied and fixed by the Contractor. Keyed winder units (coloured to match frames) are to be installed in all casement windows. All locks are to be keyed alike.
2. All external door mortise locks, concealed flush bolts and catches, as well as internal door handles and door stops are to be supplied by the Proprietor and installed by the Contractor.
3. All electrical and light switches, dimmer switches, halogen dimmer switches, double GPOs, telephone sockets, aerial sockets, plates etc, are to be supplied and fixed by the Contractor.
4. All **PC items** listed/specified in the detail drawings and/or summary sheets are to be supplied and fixed by the Contractor.
5. The Contractor will purchase all other door hardware, which will be fitted by the Contractor.
6. The Contractor is to fix all the light fittings, which will be purchased by the Proprietor.

PAINTING

1. All external woodwork is to be pre-primed, generally prior to fixing.
2. External timbers (including the front door and frame) are to be prepared as follows: sand to a smooth finish and dust off before priming. After priming, stop all holes and cracks with oil putty. When dry, sand and dust off before painting with premium quality primer followed by an undercoat, then two coats of premium paint.
3. All internal timber (architraves and skirtings) is to have all nails punched with all holes and cracks to be filled with wood filler. When dry, sand and dust off before painting with premium quality primer/sealer.
4. All internal timbers are to have one coat of undercoat (over the primer) and two finishing coats of premium paint. Type of paint (ie gloss, acrylic etc) and colour to be selected later.
5. All internal surfaces are to have holes/cracks filled and sanded smooth before being painted with premium quality primer/sealer. Finish with one coat of undercoat and two finishing coats of premium paint. Colour to be selected later.
6. All external surfaces are to be properly sanded/rubbed before being painted with a premium quality primer/sealer. Finish with two coats of premium paint.
7. All external paint shall be in accordance with the Architectural Plans.
8. Allow for the finishing of the front doors and garage door. The exact finish will be determined later.
9. All internal brick walls must be painted, except the wet areas, which will be tiled.

SUMMARY OF PLUMBING FITTINGS

Generally
The Plumber is to provide the materials and labour required for all the plumbing and drainage work shown on the architectural drawings (1:100 and 1:20 scale).
PC Allowance
The Contractor is to allow **a Prime Cost Sum of $20,000** for all of the following fixtures and fittings. The Proprietor will chose the brand, style etc of the items and inform the Contractor, who will supply and install them.
Ground Floor 1 Bathroom + Laundry:
Bathroom:
1 of hand basin in vanity unit and basin mixer tap set, 1 of **frameless** shower screen with 800mm wide hinged door, plus: 1 of showerhead and flick mixer set 1 of 900mm towel rails 1 of 1800x800 bathtub 1 of toilet roll holder 1 of shower shelf 1 of mirror as per specification

Laundry:
1 Sink with 2 bowls ad waste. 1 of washing machine tap set.

First Floor: 1 bathroom + 1 Ensuite:
Bathroom:
1 of hand basin in vanity unit and basin mixer tap set, 1 of **frameless** shower screen with 800mm wide hinged door, plus: 1 of showerhead and flick mixer set 1 of 900mm towel rails 1 of 1800x800 bathtub 1 of toilet roll holder 1 of shower shelf 1 of mirror as per specification
Ensuite:
1 of hand basin in vanity unit and basin mixer tap set, 1 of **frameless** shower screen plus: 1 of shower head and flick mixer set 1 of 900mm towel rails 1 of toilet roll holder 1 of shower shelf
1 of mirror as per specification

SUMMARY OF ELECTRICAL FITTINGS

GenerallyThe electrician is to allow for all wiring and the installation of all of the fittings shown on the ELECTRICAL LAYOUT.
An Electrical layout should be provided by the developers, unless any prior agreements have been made.

PC allowance
The Contractor is to allow a **Prime Cost Sum of $9,000** for the supply of the light fittings shown on the ELECTRICAL LAYOUT. The Proprietor will select the fittings and inform the Contractor at a later date. All other fittings are to be supplied by the Contractor, but must seek approval from the proprietor first.

FENCING

1. All fencing shall be completed as per the architectural plans.

SWIMMING POOLS

1. Swimming Pools (if applicable to the project) shall be constructed in accordance with the detailed architectural plans prepared by Cedar Designs Pty Ltd
2. Swimming Pool access is to comply with NCC Vol. 2, F 2.5.2 (A) and (B) in conjunction with the swimming pools act 1992 and the Swimming Pool regulation 2008.
3. Safety railing shall be provided around the pool at a height of 1.2m in accordance with the detailed pool plans.
4. Prior to occupation, the pool must be inspected for compliance and safety.
5. Prior to occupation, the pool must be registered. (https://www.swimmingpoolregister.nsw.gov.au/)
6. Swimming pool finish to be in accordance with the Architectural Plans.

BUSHFIRE PRONE AREAS

NCC Vol. 1 parts G 5.0, 5.1, 5. or NCC Vol. 2 part 3.7.4. Site assessment and preparation, construction of and maintenance of Class 1 buildings and decks and Class 10a buildings in a Bushfire Prone Area are required to comply with the provisions of AS3959 as applicable and BCA 3.7.4.

ALPINE AREAS

For buildings to be constructed in an alpine area, compliance with the requirements of NCC part 3.7.5. is required. Alpine areas are areas above Australian Height Datum (AHD) as follows:- NSW, VIC, ACT above 1,200 metres AHD. TASMANIA above 900 metres AHD. For sub alpine areas where significant snow loads may occur see BCA fig. 3.7.5.2. Where snow loads may be applied to a building design according to AS1170.3 is required.(see NCC 3.11.3)

CLIMATE ZONES

Climate Zone classifications for various localities are shown in NCC Vol. 2 2014 Table1.1.2. Thermal design requirements for climate zones should be as per NCC fig. 1.1.4 EARTHQUAKE: Earthquake probability shall be determined according to NCC Vol. 2 part 3.11.3 and loading requirements are to be designed to comply with AS1170.4 LANDSCAPING: The area to be landscaped shall comply with the landscape plan and requirements of the Local Council Authorities. Appropriate landscape design will reduce water usage in lawns and gardens by up to 50%. Selection of native indigenous plants suited to the local micro climate along with exotic species from California, South Africa and the Mediterranean will normally require minimal maintenance and water use. (BASIX website: see table D.2.1 for indigenous plants in various local government areas for NSW use).

EARTHQUAKE

Earthquake probability shall be determined according to NCC Vol. 2 part 3.11.3 and loading requirements are to be designed to comply with AS1170.4

DURING CONSTRUCTION

1. Where a swimming pool is to be removed, The site of the swimming pool must be filled (if necessary) so as to restore the site to the ground levels (existing) adjacent to the pool, and the swimming pool must not be filled with building demolition waste of any kind and if constructed as a concrete shell must be demolished so as to allow ground water to escape or drain to groundwater and the fill must be certified clean imported soil or virgin excavated material (VENM) and compacted, and ny piping or similar material must be removed from the site before the ste is filled.
2. Site sign - Soil & Erosion Control Measures - Prior to the commencement of works (including demolition and excavation), a durable site sign, issued by Council, must be erected in a prominent location on site.
3. The site sign warns of the penalties which apply to pollution,storing materials on road or footpath and breaches of the conditions relating to erosion and sediment controls.
4. Hours of construction for demolition and building work must be in accordance with the relevant approval unless authorised by council.
5. Where Applicable Swimming Pools - Filling with water - The pool/spa shall not filled until the safety fences have been completed in accordance with the approved plans and specifications and inspected by the PCA.
6. Ground levels and retaining walls - The ground levels of the site shall not be excavated, raised or filled, or retaining walls constructed on the allotment boundary, except where indicated on approved plans prepared by Cedar Designs Pty Ltd.

OBSTRUCTION OF ROAD OR FOOTPATH

The use of the road or footpath for the storage of any building materials, waste materials, temporary toilets, waste or skip bins, or any other matter is not permitted unless separately approved by Council under Section 138 of the Roads Act 1993 and/or under Section 68 of the Local Government Act 1993. Penalty infringement Notices may be issued for any offences and severe penalties apply.

WASTE MANAGEMENT FACILITIES

Waste Management Facility - All materials removed from the site as a result of demolition, site clearing, site preparation and, or excavation shall be disposed of at a suitable Waste Management Facility. No vegetation, article, building material, waste or the like shall be ignited or burnt.
Copies of all receipts for the disposal, or processing of all such materials shall be submitted to the PCA and Council, where Council is not the Principal Certifying Authority.

CRITICAL INSPECTIONS DURING CONSTRUCTION

All of the following inspections MUST be completed by the council or the PCA, where council is not the Principal Certifying Authority.

1. Ground Floor Footings
2. Ground Floor Slab
3. First Floor Suspended Slab or Suspended Deck (where applicable)
4. Suspended Concrete roof or roof timber framing
5. Waterproofing
6. Final Inspection prior to the issue of an occupation certificate

NOTE: Failure to comply with the above may result in a void complying development certificate or construction certificate
NOTE: Other inspections may be required depending on the project, the site developer is responsible to ensure any additional inspections are completed.
NOTE: You are advised to contact the Certifying authority for inspection a minimum of 1 week prior to ensure adequate timing is provided where rectifications may be required.

COMPLETION

1. The works shall be complete in every trade. Sashes, doors, locks etc shall be left in satisfactory operating order. Surplus materials and rubbish shall be removed from the site. The works are to be left clean and fit for occupation with all mirrors and all glass cleaned, gutters and drains cleared.
2. Obtain all the necessary / required approvals and Certificates to obtain the Occupancy Certificate from the Certifier.
3. Issue all instruction manuals and guarantee paperwork to the Proprietors.

PRIOR TO THE ISSUE OF AN OCCUPATION CERTIFICATE

1. All works must be completed in accordance with the Architectural Plans prepared by Cedar Designs Pty Ltd
2. All works must be completed in accordance with the Stormwater Plans and Structural plans relevant to the project.
3. All works must be completed in accordance with the Basix Certificate relevant to the Project.
4. Where applicable - A Section 73 Compliance Certificate under the Sydney Water Act 1994 <http://legislation.nsw.gov.au/> must be submitted to the PCA prior to the issue of the Occupation/Subdivision Certificate.
5. Where applicable - A Maintenance Schedule for the proposed on-site stormwater management measures is to be prepared and submitted to Council. The Maintenance Schedule shall outline the required maintenance works, how and when these will be done and who will be carrying out these maintenance works.
6. All the stormwater/drainage works shall be completed in accordance with the approved Construction Certificate plans or complying development plans prior to the issue of the Occupation Certificate.
7. Work as Executed Plans prepared by a Chartered Professional Engineer or a Registered Surveyor when all the site engineering works are complete shall be submitted to the PCA prior to the issue of the Occupation Certificate.
8. Stormwater drainage works - Works As Executed - Prior to the issue of the Occupation Certificate, stormwater drainage works are to be certified by a professional engineer specialising in hydraulic engineering, with Works-As Executed drawings supplied to Council detailing:
9. (a) Compliance with conditions of development consent relating to stormwater;
10. (b) The structural adequacy of the On-Site Detention system (OSD);
11. (c) That the works have been constructed in accordance with the approved design and will provide the detention storage volume and attenuation in accordance with the submitted calculations;
12. (d) Pipe invert levels and surface levels to Australian Height Datum;
13. (e) Contours indicating the direction in which water will flow over land should the capacity of the pit be exceeded in a storm event exceeding design limits.

1. BASIX Compliance Certificate - A Compliance Certificate must be provided to the PCA regarding the implementation of all energy efficiency measures as detailed in the approved BASIX Certificate before any Occupation Certificate is issued.
2. Completion of Landscape Works - All landscape works, trees planted and fees payable for Councils street tree planting must be completed before the issue of the Final Occupation Certificate and to the satisfaction of Councils Tree Management Officers.
3. Vehicular crossing e vehicular crossing and/or footpath works shall be constructed by a private contractor at the expense of the developers, in accordance with the 'Application for Driveway Crossing and Associated Works on Council Road Reserve' approval issued by Council's Assets and Infrastructure Division. Any existing vehicular crossing and/or laybacks which are redundant must be removed. The kerb and gutter, any other footpath and turf areas shall be restored at the expense of the applicant and in accordance with Council's Specification for Vehicular Crossings and Associated Works.

NOTE: No stencilled or coloured concrete may be used outside the boundary of the property unless approved otherwise by council.

The work must be completed before the issue of an Occupation Certificate.

CERTIFICATION REQUIRED PRIOR TO THE OCCUPATION CERTIFICATE

At minimum the following certificates must be provided to the PCA prior to the issue of the occupation certificate.

1. Identification Survey prepared by a registered surveyor indicating the setbacks of the front, side and rear to boundaries, finished floor levels and top of ridge levels.
2. Waterproofing certificate (must state the product used, name of the installer and number of coats)
3. Elecrtrical certification for Smoke alarms, Hard wiring and mechnical ventilation.
4. Stormwater compliance certificate issued by a licenced plumber.
5. Stormwater compliance certificate issued by the office of Fair trading for the plumbing and drainage works.
6. Termite treatment certification.
7. Glazing certification for the windows, shower screens and any balustrades.
8. Insulation and installation certificate
9. Basix compliance certificate
10. Structural certificate issued by an engineer
11. Timber framing certificate
12. Clearance certificate (for demolition works only)
13. Pool registration (where applicable)
14. Landscaping completion certificate

NOTE: Additional certificates may be required prior to the occupation certificate
NOTE: It is the responsibility of the developer to contact the PCA for additional information
NOTE: It is the responsibility of the developer to ensure all certificates are provided to the PCA via the NSW Planning Portal.

26 LUCINDA AVE, BASS HILL

CEDAR DESIGNS

IBRAHIM MUSTAPHA
BDAA ACCREDITED - 6450.
BDAA MEMBER - 2360 - 17
REGISTERED DESIGN PRACTITIONER - DEP0000079

CEDAR DESIGNS PTY LTD
EMAIL: INFO@CEDARDESIGNS.COM.AU
WEBSITE: WWW.CEDARDESIGNS.COM.AU
PHONE: +61 410 289 126

ISSUE	DESCRIPTION
A	ISSUED FOR CLIENT REVIEW

Scale: @ A2


NOTES AND SPECIFICATIONS

01/28

GENERAL NOTES
- Do not scale drawings, use figured dimensions only.
- All dimensions and levels are to be verified on site before any work commences.
- All work is to be carried out in accordance with the AS and NCC standards.

COPYRIGHT:
This document is COPYRIGHT and the property of CEDAR DESIGNS PTY LTD. It is not to be retained, copied or used without the prior written permission of CEDAR DESIGNS PTY LTD.

17/08/2026 5:20:37 PM

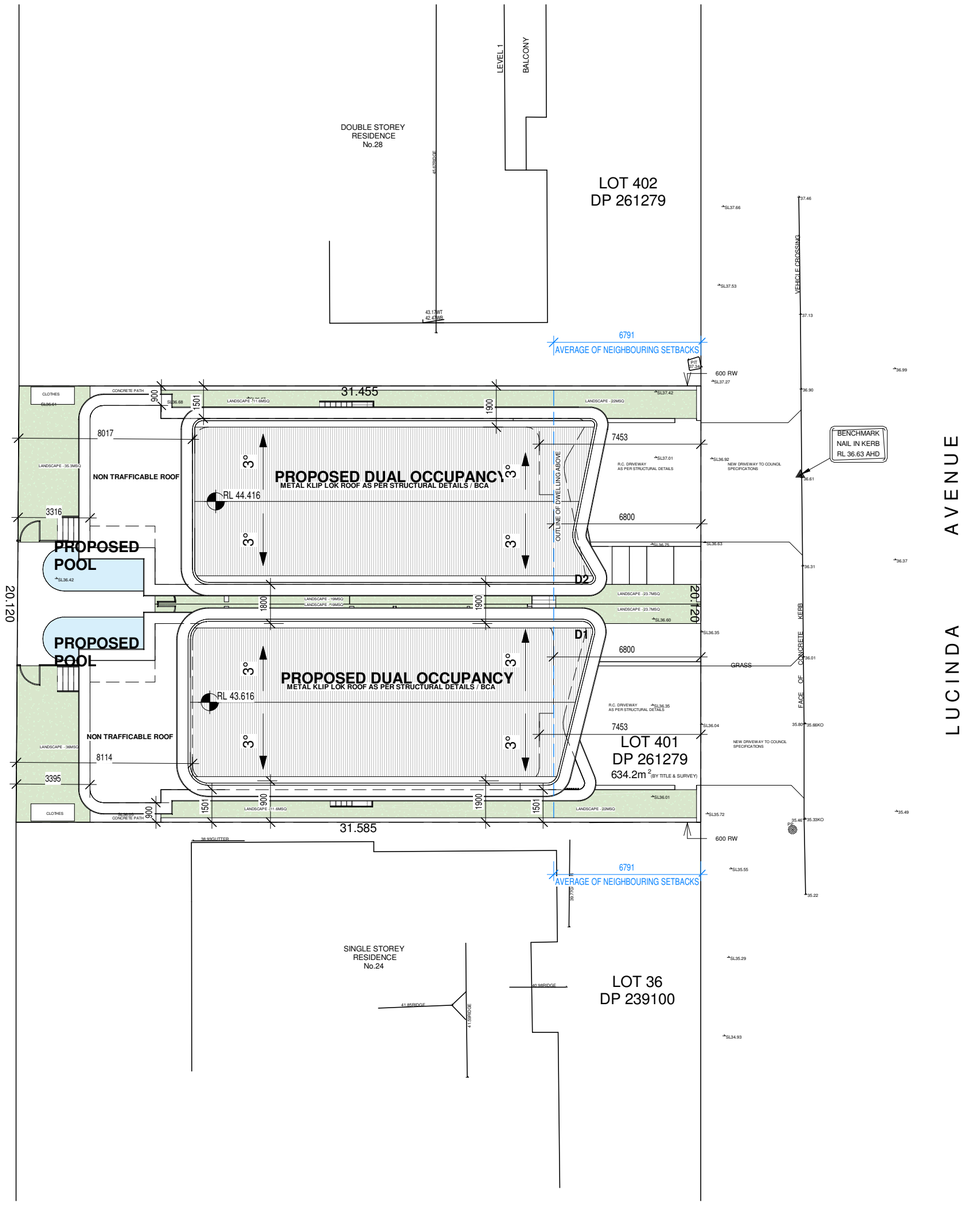

PROPOSED SITE PLAN
1 : 200

DEVELOPMENT DATA / SITE CALCULATIONS	
SITE AREA:	**- 634.2MSQ**

GROSS FLOOR AREA (GFA) CALCULATIONS:

PERMISSIBLE GFA - 458.55MSQ

DWELLING 1

BASEMENT LEVEL:	-103.3 MSQ (NOT INCLUDED IN GFA)
GROUND FLOOR:	-109.5MSQ
FIRST FLOOR:	-101.3MSQ

TOTAL GFA D1 - 210.8MSQ

DWELLING 2

BASEMENT LEVEL:	-103.3 MSQ (NOT INCLUDED IN GFA)
GROUND FLOOR:	-109.5MSQ
FIRST FLOOR:	-101.3MSQ

TOTAL GFA D2 - 210.8MSQ

TOTAL GFA D1 + D2 - 421.6MSQ

LANDSCAPE AREA CALCULATIONS:

MINIMUM LANDSCAPE - 217.1MSQ

TOTAL LANSCAPING PRPOPOSED - 223.9MSQ

BASIX COMMITMENTS

LANDSCAPING COMMITMENTS
The applicant must plant indigenous or low water use species of vegetation throughout 20 square metres of the site.

FIXTURES
The applicant must install showerheads with a minimum rating of 4 star (> 4.5 but <= 6 L/min plus spray force and/or coverage tests) in all showers in the development.

The applicant must install a toilet flushing system with a minimum rating of 6 star in each toilet in the development.

The applicant must install taps with a minimum rating of 6 star in the kitchen in the development.

The applicant must install basin taps with a minimum rating of 6 star in each bathroom in the development.

ALTERNATIVE WATER
Rainwater tank
The applicant must install a rainwater tank of at least 3000 litres on the site. This rainwater tank must meet, and be installed in accordance with, the requirements of all applicable regulatory authorities.

The applicant must configure the rainwater tank to collect rain runoff from at least 150 square metres of the roof area of the development (excluding the area of the roof which drains to any stormwater tank or private dam).
The applicant must connect the rainwater tank to:

• all toilets in the development
• the cold water tap that supplies each clothes washer in the development
• at least one outdoor tap in the development (Note: NSW Health does not recommend that rainwater be used for human consumption in areas with potable water supply.)
• a tap that is located within 10 metres of the swimming pool in the development
• a tap that is located within 10 metres of the outdoor spa in the development

Swimming Pool
The swimming pool must not have a volume greater than 35 kilolitres.
The swimming pool must be outdoors.

Outdoor Spa
The spa must not have a volume greater than 3.6 kilolitres.
The spa must have a spa cover.

THERMAL COMFORT COMMITMENTS
General features
The dwelling must be a Class 1 dwelling according to the Building Code of Australia, and must not have more than 2 storeys.

The conditioned floor area of the dwelling must not exceed 300 square metres.

The dwelling must not contain open mezzanine area exceeding 25 square metres.

The dwelling must not contain third level habitable attic room.

Floor, walls and ceiling/roof
The applicant must construct the floor(s), walls, and ceiling/roof of the dwelling in accordance with the specifications listed in the table in the basix certificate

Windows, glazed doors and skylights

The applicant must install the windows, glazed doors and shading devices described in the table below, in accordance with the specifications listed in the table. Relevant overshadowing specifications must be satisfied for each window and glazed door.

The dwelling may have 1 skylight (<0.7 square metres) which is not listed in the table.

The following requirements must also be satisfied in relation to each window and glazed door:

• For the following glass and frame types, the certifier check can be performed by visual inspection.
- Aluminium single clear
- Aluminium double (air) clear
- Timber/uPVC/fibreglass single clear
- Timber/uPVC/fibreglass double (air) clear
• For other glass or frame types, each window and glazed door must be accompanied with certification showing a U value no greaterthan that listed and a Solar Heat Gain Coefficient (SHGC) within the range of those listed. Total system U values and SHGC mustbe calculated in accordance with National Fenestration Rating Council (NFRC) conditions. Frame and glass types shown in thetable below are for reference only.

ALL WORK TO COMPLY WITH THE BCA AND AUSTRALIAN STANDARDS.

CRITICAL INSPECTIONS TO BE UNDERTAKEN BY CERTIFYING AUTHORITY FOR THE FOLLOWING:

1. Ground Floor Footings
2. Ground Floor Slab
3. First Floor Slab
4. Roof concrete Slab
5. Waterproofing Inspection
6. Final Inspection (prior to OC)

It is the responsibility of the developer to contact the certifying authority a minimum of two days prior to inspection.

Failure May result in a void Complying Development Certificate.

FOR FURTHER DETAILS PLEASE REFER TO THE ATTACHED BASIX CERTIFICATE

26 LUCINDA AVE, BASS HILL

CEDAR DESIGN

IBRAHIM MUSTAPHA
BDAA ACCREDITED - 6450
BDAA MEMBER - 2360 - 17
REGISTERED DESIGN PRACTITIONER - DEP0000079

CEDAR DESIGNS PTY LTD
EMAIL: INFO@CEDARDESIGNS.COM.AU
WEBSITE: WWW.CEDARDESIGNS.COM.AU
PHONE: +61 410 289 126


ISSUE	DESCRIPTION
A	ISSUED FOR CLIENT REVIEW

Scale: 1 : 200 @ A2 — PROPOSED SITE PLAN — 02/28

GENERAL NOTES
- Do not scale drawings, use figured dimensions only.
- All dimensions and levels are to be verified on site before any work commences.
- All work is to be carried out in accordance with the AS and NCC standards.

COPYRIGHT:
This document is COPYRIGHT and the property of CEDAR DESIGNS PTY LTD. It is not to be retained, copied or used without the prior written permission of CEDAR DESIGNS PTY LTD.

17/08/2026 5:20:37 PM

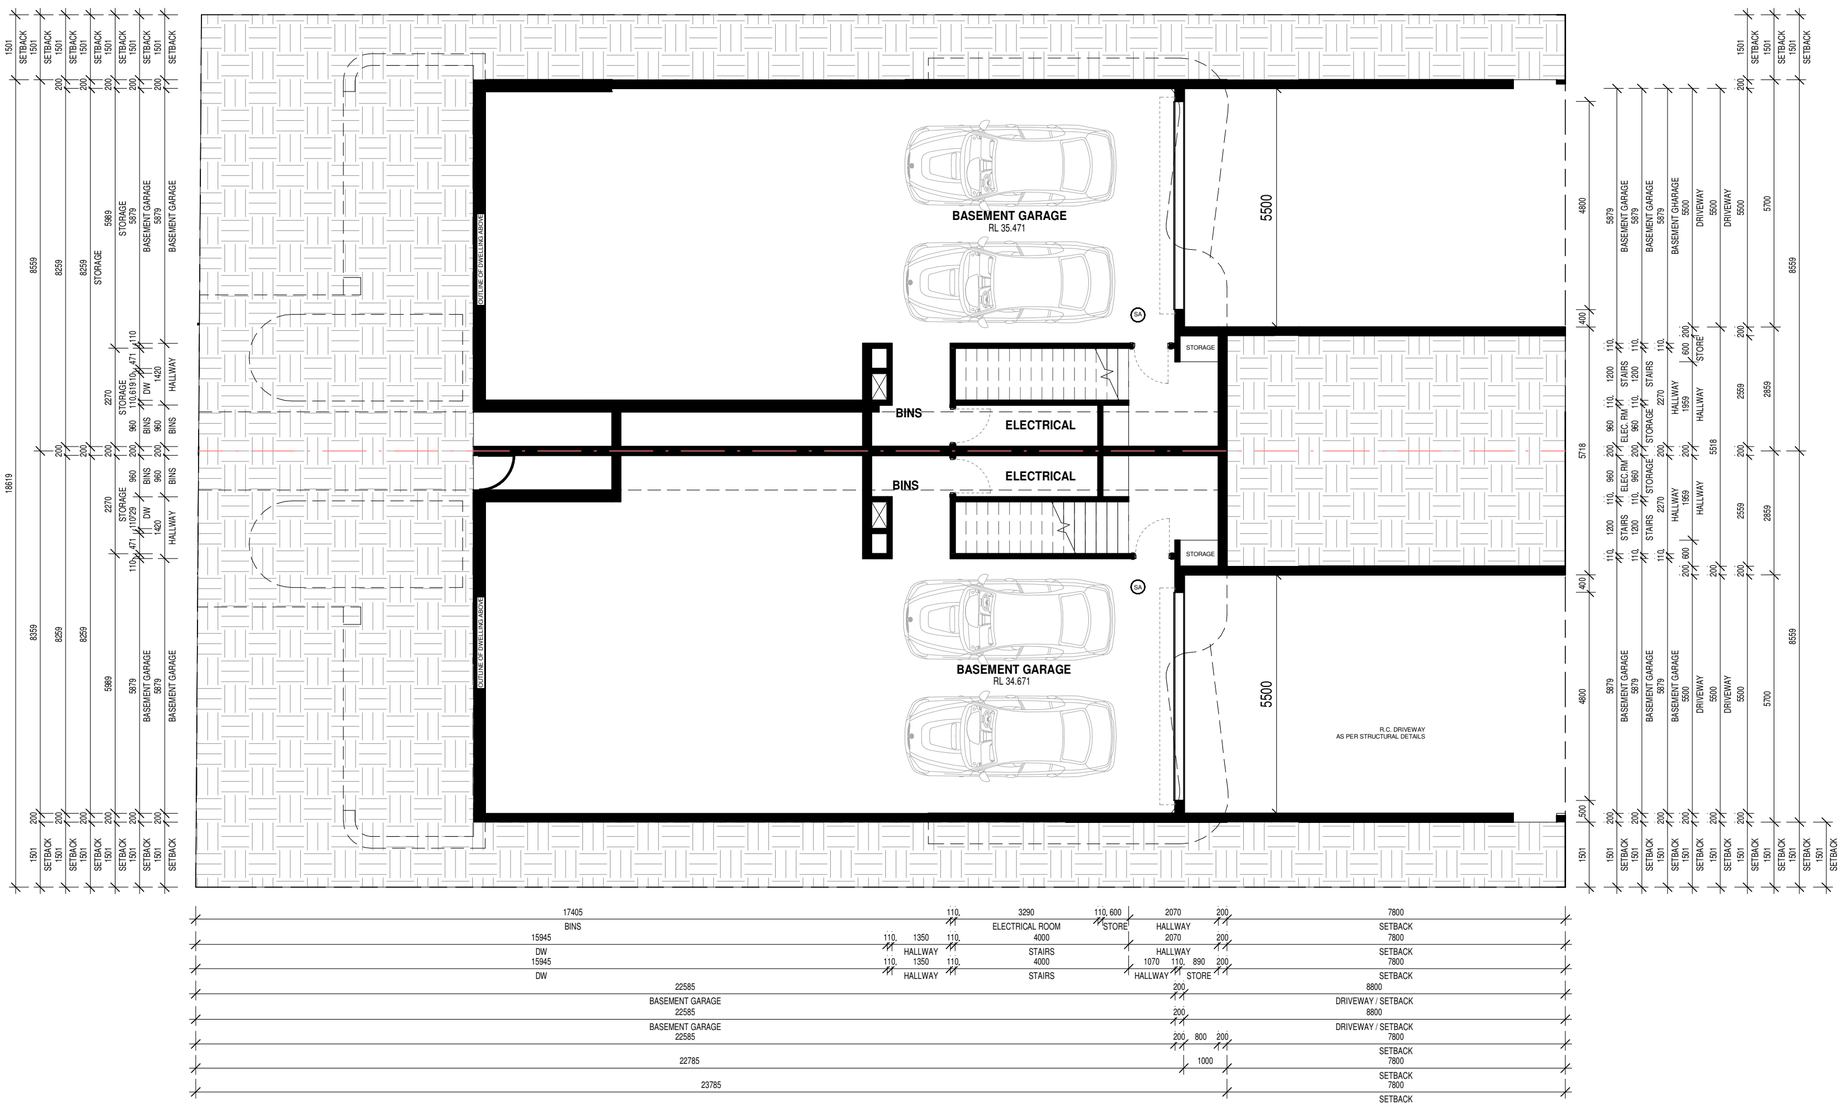

NOTES:

Air-conditioning units shall be installed in accordance with the relevant provisions of the NCC 2022, including Volume Two, Part 2.7 (Health and Amenity), and shall comply with the maximum permissible noise levels as outlined in Objective 2.1P1 and any applicable local council requirements.

All handrails and balustrades shall be designed and constructed in accordance with NCC 2022, Volume Two, Part 3.9.2, ensuring compliance with the relevant structural and safety performance requirements.

WATERPROOFING:

"All waterproofing works shall comply with NCC Volume Two (Housing Provisions), Part 10.2 and AS 3740:2021 – Waterproofing of Domestic Wet Areas. Works must be carried out by a licensed waterproofing contractor."

STEP DOWN FOR WET AREAS:

All wet areas (bathrooms, laundries, shower recesses) shall have a minimum step down of 25mm from adjoining dry floor surfaces to prevent water ingress, in accordance with AS 3740-2021 Waterproofing of domestic wet areas and NCC Vol. 2.

The step down shall be waterproofed with an approved membrane extending up the walls as required.

Thresholds or rebates shall be provided at entry points to wet areas to contain water within the wet area.

Floor falls within wet areas must be a minimum of 1:100 slope to drainage points to ensure proper water run-off.

WALL NOTES:

W1 External Walls:
270 mm double brick cavity (110 mm outer skin + 50 mm cavity + 110 mm inner skin). External finish face brick/render. Internal finish plaster set or plasterboard.

W2 Internal Walls:
110 mm single brick. Plaster set or plasterboard finish.

Proposed Basement Level

1 : 100

LEGEND & NOTES

- SELECTED OUTDOOR TILES
- SELECTED STONE CLAD
- CONCRETE
- LANDSCAPED AREA (LAWN)
- PROPOSED POOL
- SELECTED TIMBER CLAD
- SELECTED FACE BRICK
- TREE TO BE REMOVED
- TREE TO BE RETAINED

SA	SMOKE ALARM
R	RISER
LC	LAUNDRY SHUTE
SSL	SLAB LEVEL
FFL	FINISHED FLOOR LEVEL
GFA	GINISHS FLOOR AREA
FA	FLOOR AREA
F	FRIDGE
RL	RELATIVE LEVEL
AHD	AUSTRALIAN HEIGHT DATUM
RC	REINFORCED CONCRETE

26 LUCINDA AVE, BASS HILL

ISSUE	DESCRIPTION
A	ISSUED FOR CLIENT REVIEW

Scale: As indicated @ A2

PROPOSED BASEMENT PLAN

06/28

CEDAR DESIGNS

IBRAHIM MUSTAPHA
BDAA ACCREDITED - 6450
BDAA MEMBER - 2360 - 17
REGISTERED DESIGN PRACTITIONER - DEP0000079

CEDAR DESIGNS PTY LTD
EMAIL: INFO@CEDARDESIGNS.COM.AU
WEBSITE: WWW.CEDARDESIGNS.COM.AU
PHONE: +61 410 289 126

GENERAL NOTES
- Do not scale drawings, use figured dimensions only.
- All dimensions and levels are to be verified on site before any work commences.
- All work is to be carried out in accordance with the AS and NCC standards.

COPYRIGHT:
This document is COPYRIGHT and the property of CEDAR DESIGNS PTY LTD. It is not to be retained, copied or used without the prior written permission of CEDAR DESIGNS PTY LTD.

17/08/2026 5:20:38 PM



NOTES:

Air-conditioning units shall be installed in accordance with the relevant provisions of the NCC 2022, including Volume Two, Part 2.7 (Health and Amenity), and shall comply with the maximum permissible noise levels as outlined in Objective 2.1P1 and any applicable local council requirements.

All handrails and balustrades shall be designed and constructed in accordance with NCC 2022, Volume Two, Part 3.9.2, ensuring compliance with the relevant structural and safety performance requirements.

WATERPROOFING:

"All waterproofing works shall comply with NCC Volume Two (Housing Provisions), Part 10.2 and AS 3740:2021 – Waterproofing of Domestic Wet Areas. Works must be carried out by a licensed waterproofing contractor."

STEP DOWN FOR WET AREAS:

All wet areas (bathrooms, laundries, shower recesses) shall have a minimum step down of 25mm from adjoining dry floor surfaces to prevent water ingress, in accordance with AS 3740-2021 Waterproofing of domestic wet areas and NCC Vol. 2.

The step down shall be waterproofed with an approved membrane extending up the walls as required.

Thresholds or rebates shall be provided at entry points to wet areas to contain water within the wet area.

Floor falls within wet areas must be a minimum of 1:100 slope to drainage points to ensure proper water run-off.

WALL NOTES:

W1 External Walls:
270 mm double brick cavity (110 mm outer skin + 50 mm cavity + 110 mm inner skin). External finish face brick/render. Internal finish plaster set or plasterboard.

W2 Internal Walls:
110 mm single brick. Plaster set or plasterboard finish.

PROPOSED GROUND FLOOR PLAN

1 : 100

LEGEND & NOTES

- SELECTED OUTDOOR TILES
- SELECTED STONE CLAD
- CONCRETE
- LANDSCAPED AREA (LAWN)
- PROPOSED POOL
- SELECTED TIMBER CLAD
- SELECTED FACE BRICK
- TREE TO BE REMOVED
- TREE TO BE RETAINED
- SA SMOKE ALARM

R	RISER
LC	LAUNDRY SHUTE
S/L	SLAB LEVEL
FFL	FINISHED FLOOR LEVEL
GFA	GROSS FLOOR AREA
FA	FLOOR AREA
F	FRIDGE
RL	RELATIVE LEVEL
AHD	AUSTRALIAN HEIGHT DATUM
RC	REINFORCED CONCRETE

26 LUCINDA AVE, BASS HILL

ISSUE	DESCRIPTION
A	ISSUED FOR CLIENT REVIEW

Scale: As indicated @ A2

PROPOSED GROUND FLOOR PLAN

07/28

17/08/2026 5:20:39 PM


CEDAR DESIGNS

IBRAHIM MUSTAPHA
BDAA ACCREDITED - 6450
BDAA MEMBER - 2360 - 17
REGISTERED DESIGN PRACTITIONER - DEP0000079

CEDAR DESIGNS PTY LTD
EMAIL: INFO@CEDARDESIGNS.COM.AU
WEBSITE: WWW.CEDARDESIGNS.COM.AU
PHONE: +61 410 289 126

GENERAL NOTES
- Do not scale drawings, use figured dimensions only.
- All dimensions and levels are to be verified on site before any work commences.
- All work is to be carried out in accordance with the AS and NCC standards.

COPYRIGHT:
This document is COPYRIGHT and the property of CEDAR DESIGNS PTY LTD. It is not to be retained, copied or used without the prior written permission of CEDAR DESIGNS PTY LTD.

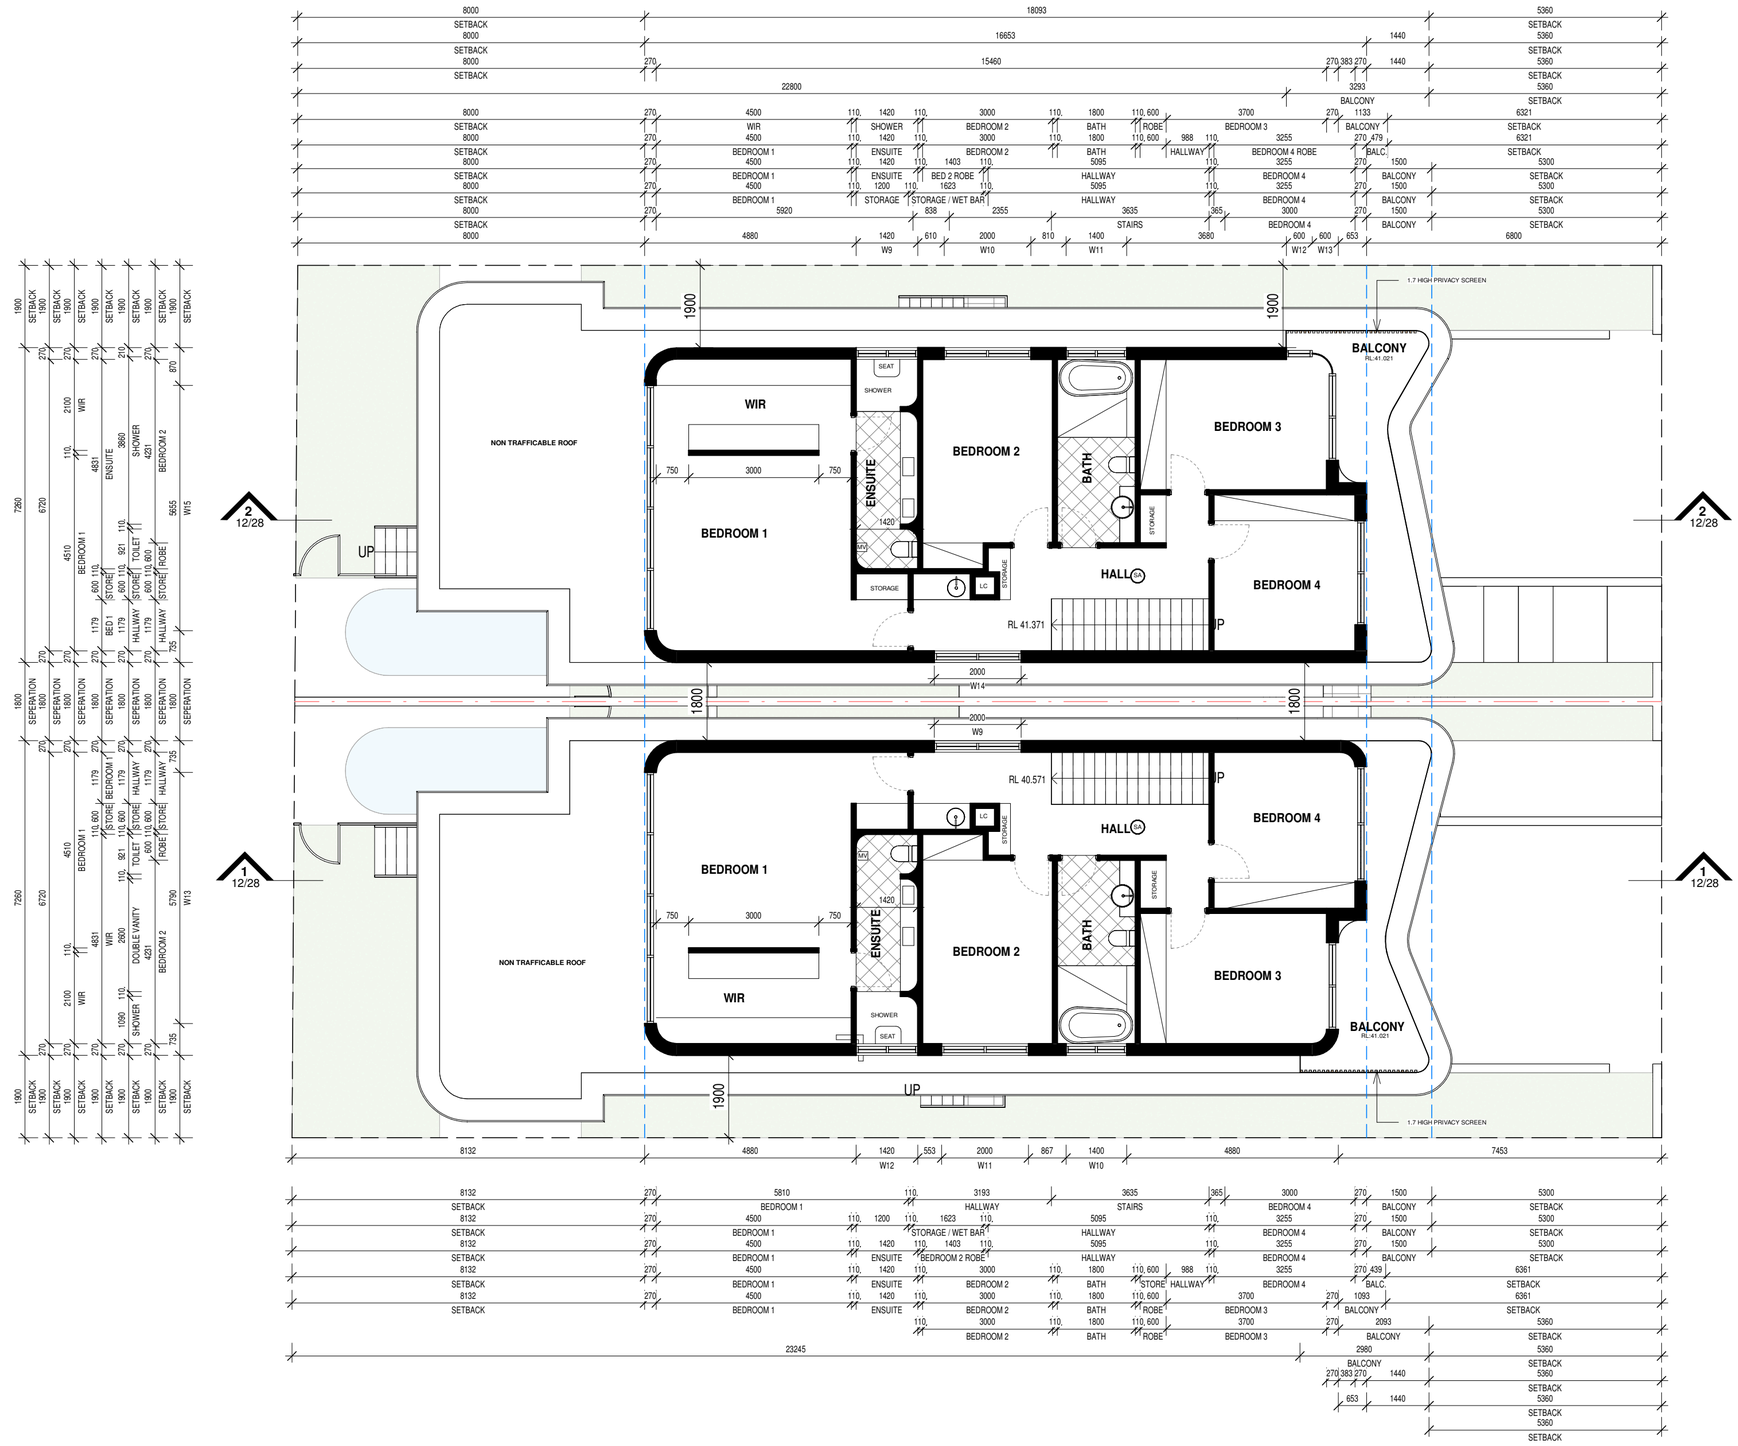

PROPOSED FIRST FLOOR PLAN

1 : 100

LEGEND & NOTES

- SELECTED OUTDOOR TILES
- SELECTED STONE CLAD
- CONCRETE
- LANDSCAPED AREA (LAWN)
- PROPOSED POOL
- SELECTED TIMBER CLAD
- SELECTED FACE BRICK
- TREE TO BE REMOVED
- TREE TO BE RETAINED

- SA SMOKE ALARM
- R RISER
- LC LAUNDRY SHUTE
- S/L SLAB LEVEL
- FFL FINISHED FLOOR LEVEL
- GFA GROSS FLOOR AREA
- FA FLOOR AREA
- F FRIDGE
- RL RELATIVE LEVEL
- AHD AUSTRALIAN HEIGHT DATUM
- RC REINFORCED CONCRETE

NOTES:

Air-conditioning units shall be installed in accordance with the relevant provisions of the NCC 2022, including Volume Two, Part 2.7 (Health and Amenity), and shall comply with the maximum permissible noise levels as outlined in Objective 2.1P1 and any applicable local council requirements.

All handrails and balustrades shall be designed and constructed in accordance with NCC 2022, Volume Two, Part 3.9.2, ensuring compliance with the relevant structural and safety performance requirements.

WATERPROOFING:

"All waterproofing works shall comply with NCC Volume Two (Housing Provisions), Part 10.2 and AS 3740:2021 – Waterproofing of Domestic Wet Areas. Works must be carried out by a licensed waterproofing contractor."

STEP DOWN FOR WET AREAS:

All wet areas (bathrooms, laundries, shower recesses) shall have a minimum step down of 25mm from adjoining dry floor surfaces to prevent water ingress, in accordance with AS 3740-2021 Waterproofing of domestic wet areas and NCC Vol. 2.

The step down shall be waterproofed with an approved membrane extending up the walls as required.

Thresholds or rebates shall be provided at entry points to wet areas to contain water within the wet area.

Floor falls within wet areas must be a minimum of 1:100 slope to drainage points to ensure proper water run-off.

WALL NOTES:

W1 External Walls:
270 mm double brick cavity (110 mm outer skin + 50 mm cavity + 110 mm inner skin). External finish face brick/render. Internal finish plaster set or plasterboard.

W2 Internal Walls:
110 mm single brick. Plaster set or plasterboard finish.

26 LUCINDA AVE, BASS HILL

CEDAR DESIGNS

IBRAHIM MUSTAPHA
BDAA ACCREDITED - 6450
BDAA MEMBER - 2360 - 17
REGISTERED DESIGN PRACTITIONER - DEP0000079

CEDAR DESIGNS PTY LTD
EMAIL: INFO@CEDARDESIGNS.COM.AU
WEBSITE: WWW.CEDARDESIGNS.COM.AU
PHONE: +61 410 289 126

ISSUE	DESCRIPTION
A	ISSUED FOR CLIENT REVIEW

Scale: As indicated @ A2


PROPOSED FIRST FLOOR PLAN

08/28

17/08/2026 5:20:40 PM

GENERAL NOTES
- Do not scale drawings, use figured dimensions only.
- All dimensions and levels are to be verified on site before any work commences.
- All work is to be carried out in accordance with the AS and NCC standards.

COPYRIGHT:
This document is COPYRIGHT and the property of CEDAR DESIGNS PTY LTD. It is not to be retained, copied or used without the prior written permission of CEDAR DESIGNS PTY LTD.

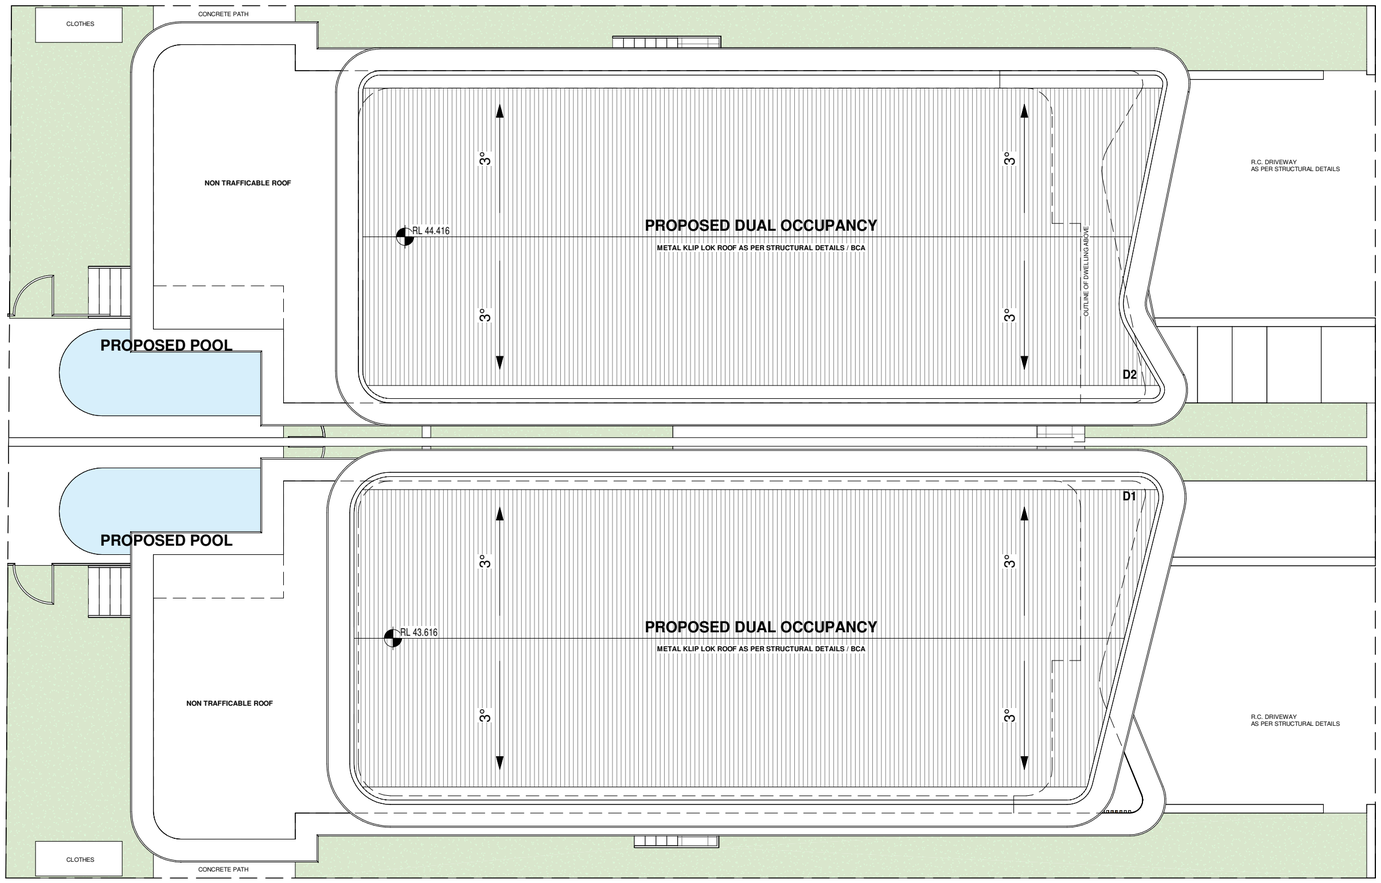

ROOF PLAN
1 : 100

ROOF CONSTRUCTION NOTES:

Metal Klip Lok roof construction to be carried out in accordance with structural engineer's details and specifications.

Roof construction to comply with the National Construction Code (NCC) 2022 requirements, including structural performance, weatherproofing, and thermal performance provisions.

All roofing elements and insulation to be designed and installed in accordance with the BASIX Certificate commitments, including thermal performance and energy efficiency requirements.

SKYLIGHT COMPLIANCE NOTES (DUAL OCCUPANCY – NSW)
Including Fire & Boundary Requirements

General Compliance
"All skylights and roof windows to comply with NCC Volume Two (Housing Provisions), Clause 9.3.2 (Roof Openings), AS 4285:2007 – Skylights, and manufacturer specifications."

Non-Combustibility & Boundary Proximity
"Where a skylight or roof window is located within 900mm of a boundary (or within a fire separation zone as per NCC Part 10.7), the following fire protection measures must apply:"

"The skylight must be constructed from non-combustible materials or materials that achieve compliance with AS 1530.1 (Combustibility Test for Materials)."

"Glazing must be Grade A safety glass that is toughened and non-combustible, or tested and deemed to comply under AS 3959 for bushfire or NCC Specification 2.7 for fire-resisting construction."

"No openings permitted within 900mm of the boundary unless protected by compliant fire shutters or external screens tested to AS 1530.4."

"Flashings, fixings, and frames must also be non-combustible if within 900mm of the boundary."

Thermal & BASIX Compliance
"All skylights must meet thermal performance values required under BASIX and NCC Section J, including use of double glazing or low-E coatings where specified."

"Skylights used for daylighting credits must provide minimum daylight levels to habitable rooms."

Ventilation & Smoke
"Operable skylights used for natural ventilation must comply with NCC Part 10.8 and provide effective cross-ventilation."

"If used for smoke relief, operable skylights must be automated and comply with AS 1668.1 (where applicable)."

Safety Glazing
"Skylights installed over stair voids or in trafficable locations must be safety glazed in accordance with AS 1288 – Glass in Buildings."

Execution & Certification
"Installation must be carried out by qualified trades and in accordance with manufacturer guidelines."

"Final inspection and compliance certificate to be provided prior to occupation."

Installation & Weatherproofing
"All skylights must be installed with fully sealed flashings to prevent water ingress."

"Roof structure to be framed to maintain structural integrity and support skylight loads."

"Roof membrane and insulation must be reinstated and sealed properly around skylight openings."

26 LUCINDA AVE, BASS HILL

CEDAR DESIGNS

IBRAHIM MUSTAPHA
BDAA ACCREDITED - 6450
BDAA MEMBER - 2360 - 17
REGISTERED DESIGN PRACTITIONER - DEP0000079

CEDAR DESIGNS PTY LTD
EMAIL: INFO@CEDARDESIGNS.COM.AU
WEBSITE: WWW.CEDARDESIGNS.COM.AU
PHONE: +61 410 289 126

ISSUE	DESCRIPTION
A	ISSUED FOR CLIENT REVIEW

Scale: 1 : 100 @ A2

PROPOSED ROOF PLAN

09/28

GENERAL NOTES
- Do not scale drawings, use figured dimensions only.
- All dimensions and levels are to be verified on site before any work commences.
- All work is to be carried out in accordance with the AS and NCC standards.


COPYRIGHT:
This document is COPYRIGHT and the property of CEDAR DESIGNS PTY LTD. It is not to be retained, copied or used without the prior written permission of CEDAR DESIGNS PTY LTD.

17/08/2026 5:20:41 PM

NOTES:


All handrails and balustrades shall be designed and constructed in accordance with National Construction Code (NCC) 2022, Volume Two, Part 3.9.2, ensuring compliance with safety, height, and load requirements.

Protection of openable windows (including window safety devices or barriers) shall comply with NCC 2022, Volume Two, Part 3.9.2.6, ensuring guard requirements are met where fall-risk applies.

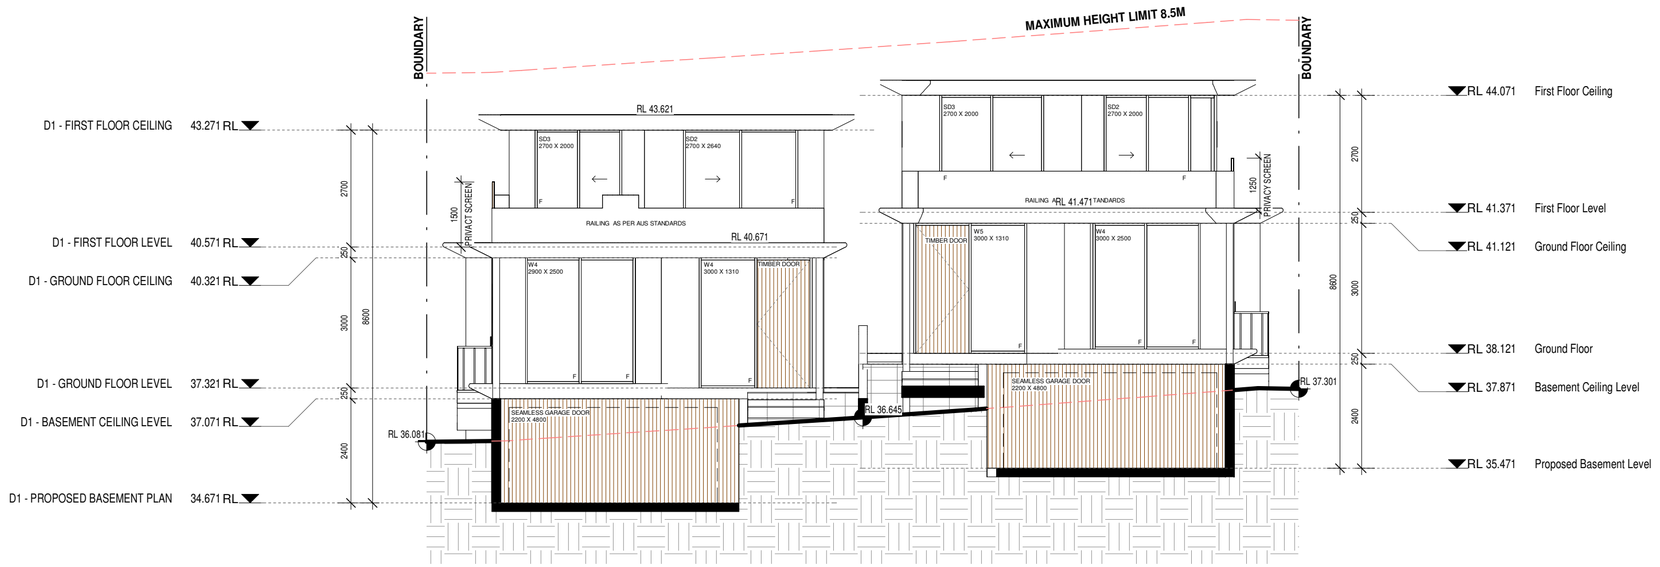


NORTH EAST ELEVATION

1 : 100

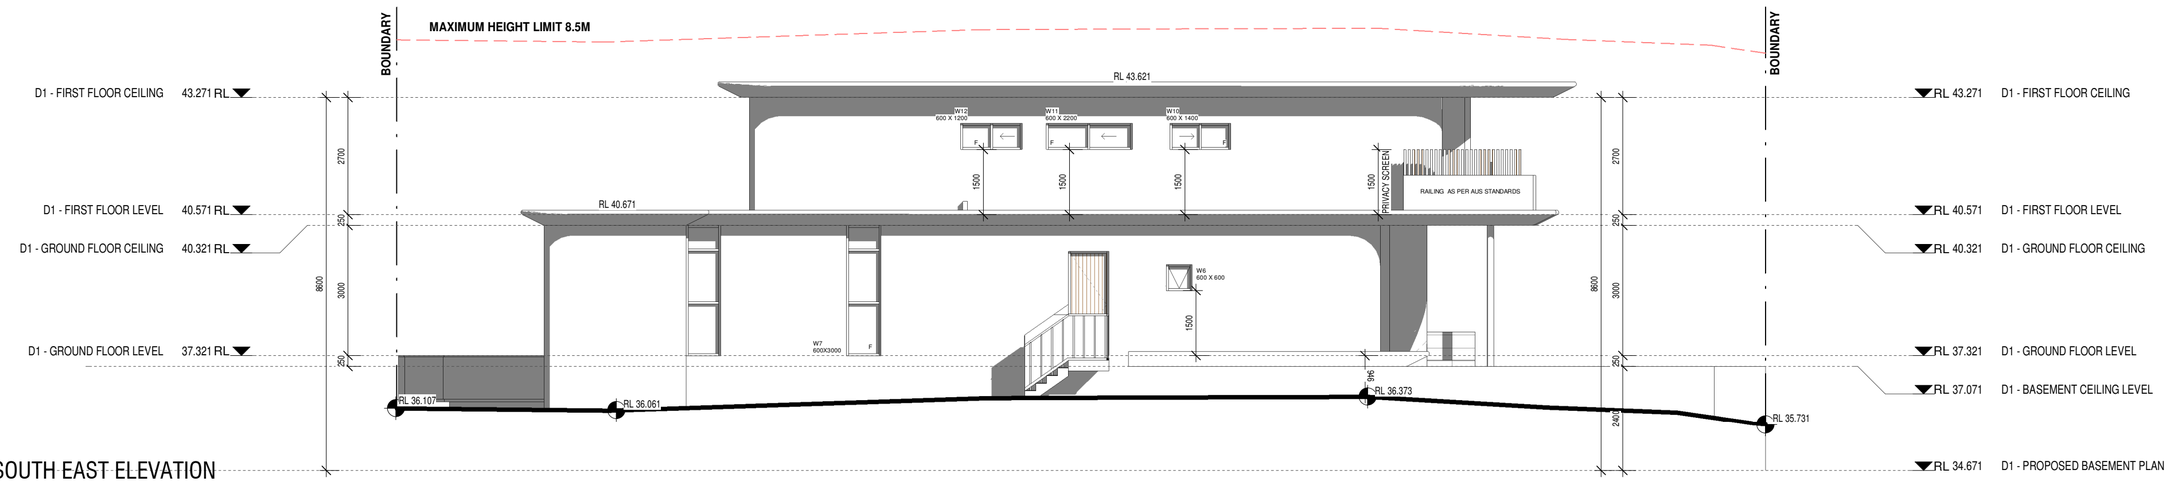

SOUTH EAST ELEVATION

1 : 100

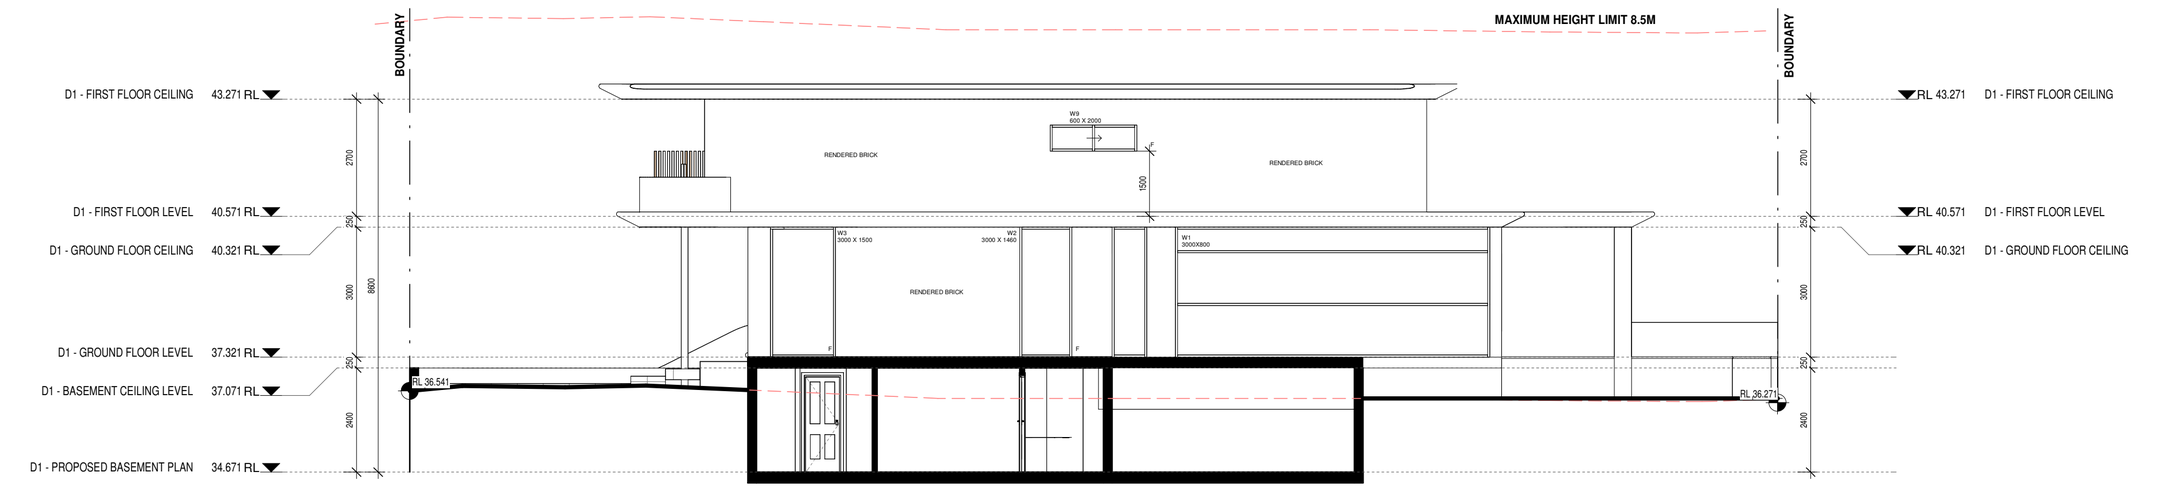

DWELLING 2 SOUTH WEST ELEVATION1

1 : 100

26 LUCINDA AVE, BASS HILL

CEDAR DESIGNS

ISSUE	DESCRIPTION
A	ISSUED FOR CLIENT REVIEW

Scale: 1 : 100 @ A2

BUILDING ELEVATIONS 1

10/28

IBRAHIM MUSTAPHA
BDAA ACCREDITED - 6450
BDAA MEMBER - 2360 - 17
REGISTERED DESIGN PRACTITIONER - DEP0000079

CEDAR DESIGNS PTY LTD
EMAIL: INFO@CEDARDESIGNS.COM.AU
WEBSITE: WWW.CEDARDESIGNS.COM.AU
PHONE: +61 410 289 126

GENERAL NOTES
- Do not scale drawings, use figured dimensions only.
- All dimensions and levels are to be verified on site before any work commences.
- All work is to be carried out in accordance with the AS and NCC standards.


COPYRIGHT:
This document is COPYRIGHT and the property of CEDAR DESIGNS PTY LTD. It is not to be retained, copied or used without the prior written permission of CEDAR DESIGNS PTY LTD.

17/08/2026 5:20:42 PM


NOTES:

All handrails and balustrades shall be designed and constructed in accordance with National Construction Code (NCC) 2022, Volume Two, Part 3.9.2, ensuring compliance with safety, height, and load requirements.


Protection of openable windows (including window safety devices or barriers) shall comply with NCC 2022, Volume Two, Part 3.9.2.6, ensuring guard requirements are met where fall-risk applies.

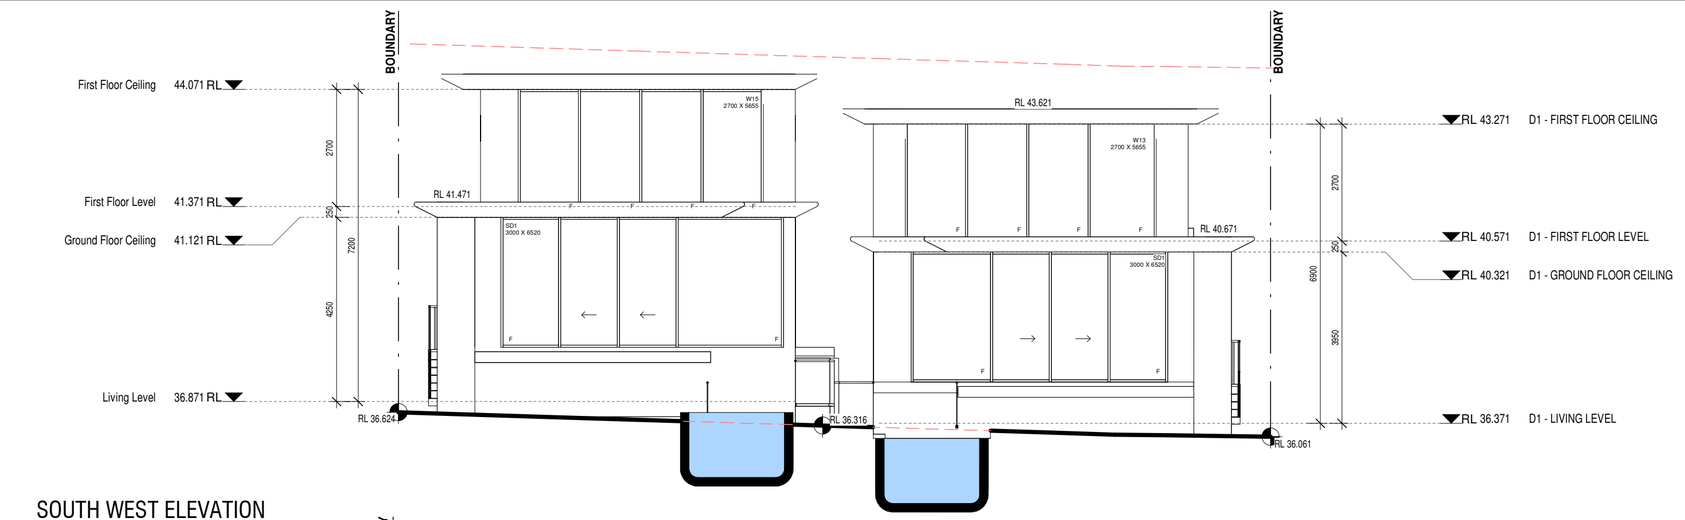

SOUTH WEST ELEVATION
1 : 100

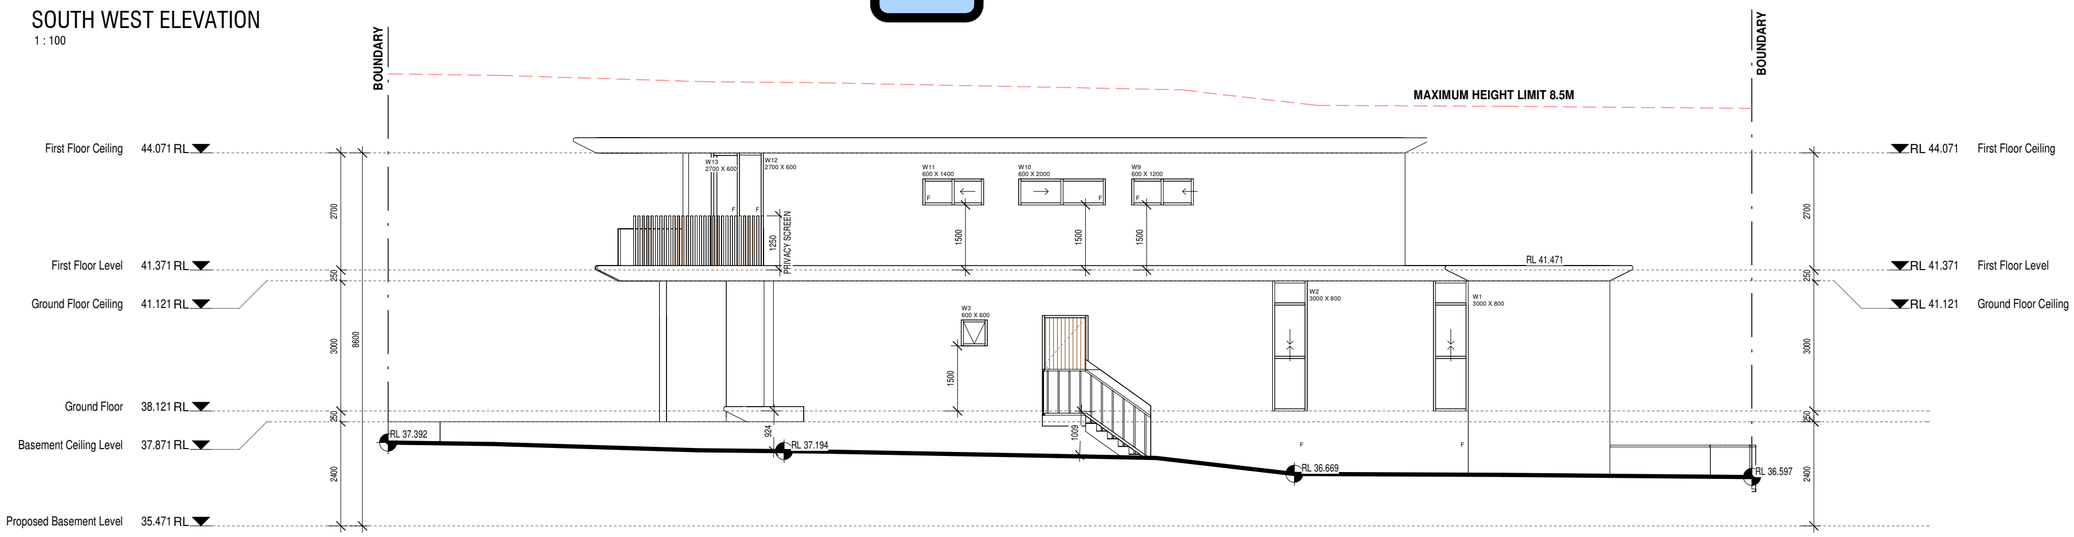

NORTH WEST ELEVATION
1 : 100

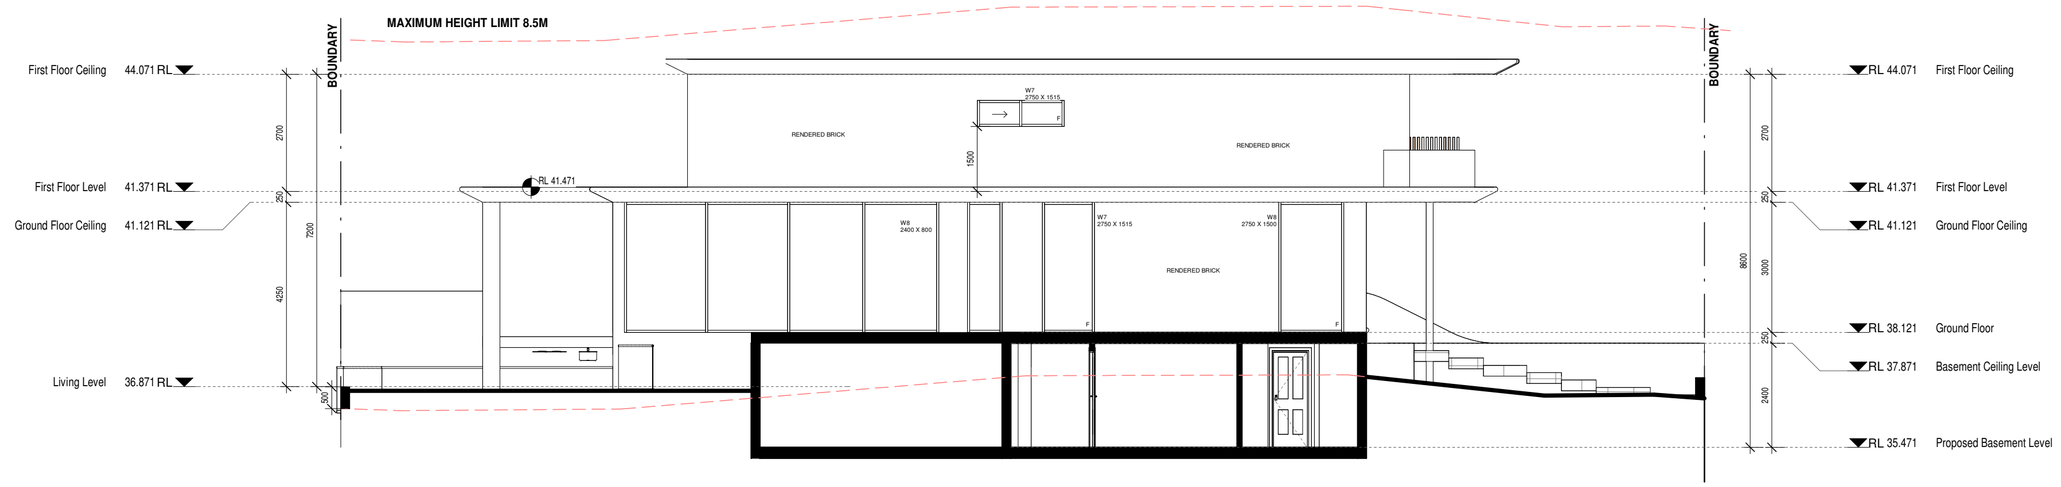

DWELLING 2 SOUTH WEST ELEVATION
1 : 100

26 LUCINDA AVE, BASS HILL

CEDAR DESIGN

IBRAHIM MUSTAPHA
BDAA ACCREDITED - 6450
BDAA MEMBER - 2360 - 17
REGISTERED DESIGN PRACTITIONER - DEP0000079

CEDAR DESIGNS PTY LTD
EMAIL: INFO@CEDARDESIGNS.COM.AU
WEBSITE: WWW.CEDARDESIGNS.COM.AU
PHONE: +61 410 289 126

ISSUE	DESCRIPTION
A	ISSUED FOR CLIENT REVIEW

Scale: 1 : 100 @ A2


BUILDING ELEVATIONS 2

11/28


GENERAL NOTES
- Do not scale drawings, use figured dimensions only.
- All dimensions and levels are to be verified on site before any work commences.
- All work is to be carried out in accordance with the AS and NCC standards.

COPYRIGHT:
This document is COPYRIGHT and the property of CEDAR DESIGNS PTY LTD. It is not to be retained, copied or used without the prior written permission of CEDAR DESIGNS PTY LTD.

17/08/2026 5:20:43 PM

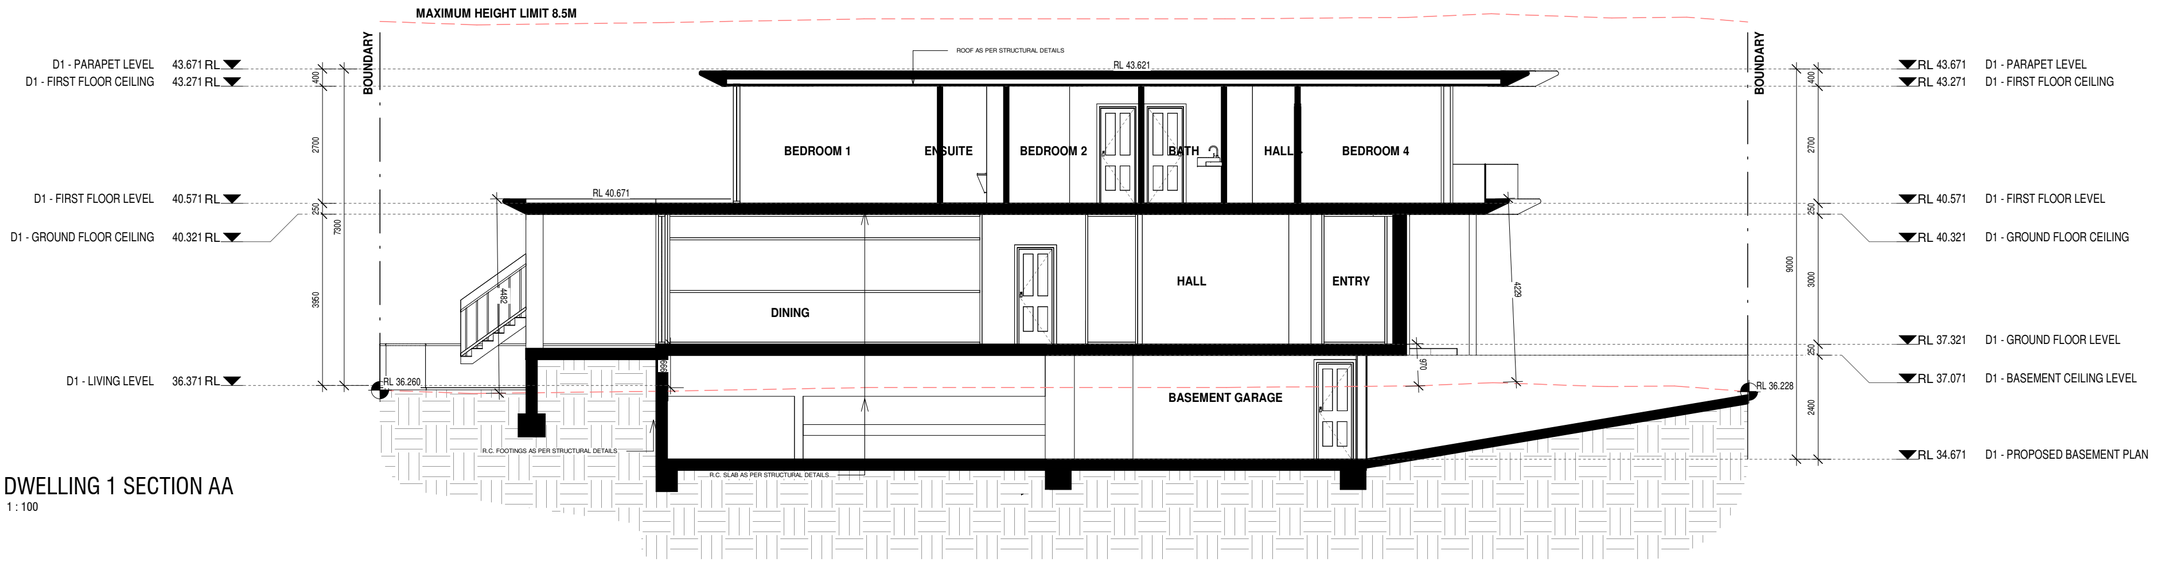

DWELLING 1 SECTION AA
1 : 100

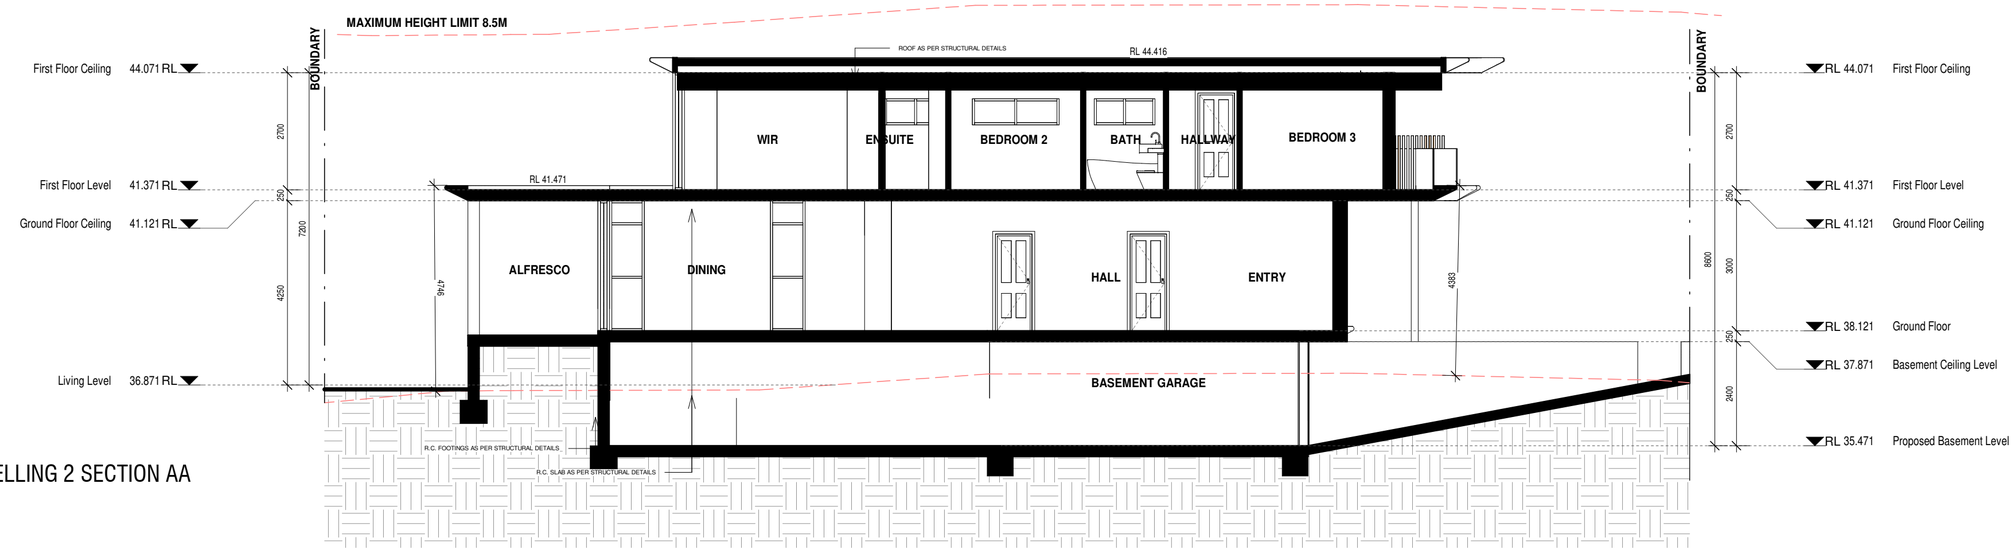

DWELLING 2 SECTION AA
1 : 100

PARTY WALL COMPLIANCE NOTES (CLASS 1 BUILDINGS IN NSW)

General Compliance Note
"All party walls (separating walls) between dwellings shall comply with the National Construction Code (NCC) Volume Two – Part 10.7 (Fire Separation), and Clause 3.7.1 for Fire-Resisting Construction, and where applicable, be constructed in accordance with NCC Specification 2.7 or 3.7.1.8."

Fire Resistance & Construction Notes
"Party walls shall achieve a minimum FRL (Fire Resistance Level) of 60/60/60 from both sides and shall extend from the footings/slab to underside of the roof covering."

"Party walls shall be constructed from non-combustible materials such as core-filled concrete block, solid masonry, or fire-rated lightweight systems tested to AS 1530.4."

"No openings, penetrations or services shall be located within the separating wall unless protected in accordance with NCC Clause 10.7.1 and AS 4072.1."

"Where lightweight fire-rated systems are used, they must be constructed in accordance with the tested system requirements and installed by qualified trades."

Roof Space & Termination Notes
"Party walls must extend through the roof space to underside of non-combustible roofing or terminate at the underside of a non-combustible capping material in accordance with NCC requirements."

"Where the separating wall does not extend through the roof, a fire-rated barrier must be installed in the roof space to prevent fire spread between dwellings."

Acoustic Performance Note (if required)
"Party walls to comply with the acoustic requirements of NCC Part 10.8 and provide a minimum Rw + Ctr of not less than 50 between dwellings."

Execution & Certification Notes
"Party wall construction to be inspected and certified by the builder or certifier prior to lining or cladding."

"All works must be carried out in accordance with relevant Australian Standards including AS 3700 (masonry), AS 1530.4 (fire tests), and AS 4072.1 (penetration seals)."

STEP DOWN FOR WET AREAS

All wet areas (bathrooms, laundries, shower recesses) shall have a minimum step down of 25mm from adjoining dry floor surfaces to prevent water ingress, in accordance with AS 3740-2021 Waterproofing of domestic wet areas and NCC Vol. 2.

The step down shall be waterproofed with an approved membrane extending up the walls as required.

Thresholds or rebates shall be provided at entry points to wet areas to contain water within the wet area.

Floor falls within wet areas must be a minimum of 1:100 slope to drainage points to ensure proper water run-off.

Earthworks to comply with NCC 2022 Volume Two, Part 3.1.1.

Footings and slabs to comply with NCC 2022 Volume Two, Part 3.2, AS 2870, and structural engineer's design and certification.

Masonry and masonry weatherproofing to comply with NCC 2022 Volume Two, Part 3.3, AS 3700, and AS 4773.1 & AS 4773.2.

Timber framing to comply with NCC 2022 Volume Two, Part 3.4.0 and AS 1684.2 & AS 1684.4.

Roof cladding to comply with NCC 2022 Volume Two, Part 3.5.1, AS 2049, and AS 2050.

Gutters and downpipes to comply with NCC 2022 Volume Two, Part 3.5.2 and AS/NZS 3500.3.

All stairs to comply with NCC 2022 Volume Two, Part 3.9.1. Specific design certifications to be provided.

All handrails and balustrades to comply with NCC 2022 Volume Two, Part 3.9.2.

All habitable rooms to comply with NCC 2022 Volume Two, Part 3.8.2 (minimum ceiling heights).

All building works to comply with NCC 2022 Volume Two, Part 3.8.6 (sound insulation requirements).

GENERAL COMPLIANCE NOTES:
All building works shall comply with the National Construction Code (NCC) 2022 – Volume Two and all relevant Australian Standards, including but not limited to the following:

Site & Structural Works
Earthworks: NCC Part 3.1.1

Surface Water & Stormwater Drainage: NCC Part 3.1.2 & AS/NZS 3500.3

Termite Risk Management: NCC Part 3.1.3 & AS 3660.1

Footings and Slabs: NCC Part 3.2 & AS 2870, in accordance with Structural Engineer's design and certification

Masonry Construction & Weatherproofing: NCC Part 3.3 & AS 3700, AS 4773.1 & AS 4773.2

Framing & Roofing
Timber Framing: NCC Part 3.4.0 & AS 1684

Steel Framing: NCC Part 3.4.2

Roof Cladding: NCC Part 3.5.1 & AS 2049, AS 2050

Gutters & Downpipes: NCC Part 3.5.2 & AS/NZS 3500.3

Building Interiors
Minimum Ceiling Heights (Habitable Rooms): NCC Part 3.8.2 – minimum 2.4 m

Wet Areas & Waterproofing: NCC Part 3.8.1 & AS 3740 – to be installed with a 7-year warranty

Facilities (e.g., kitchens, bathrooms): NCC Part 3.8.3

Lighting: NCC Part 3.8.4

Ventilation: NCC Part 3.8.5

Condensation Management: NCC Part 3.8.7

Safety & Compliance
Stairs: NCC Part 3.9.1

Handrails & Balustrades: NCC Part 3.9.2

Protection of Openable Windows: NCC Clause 3.9.2.6

Glazing: NCC Part 3.6 & AS 1288

Smoke Alarms: NCC Part 3.7.2, AS 3786:2014 & hard-wired in accordance with AS 3000

Heating Appliances (if applicable): NCC Part 3.7.3

All works must comply with the following:

Termite risk management to comply with NCC 2022 Volume Two, Part 3.1.3 and AS 3660.1-2000.

Glazing to comply with NCC 2022 Volume Two, Part 3.6 and AS 1288.

Smoke alarms to comply with NCC 2022 Volume Two, Part 3.7.2, AS 3786-2014, and be hard-wired in accordance with AS 3000.

Wet areas and waterproofing to comply with NCC 2022 Volume Two, Part 3.8 and AS 3740, including a minimum 7-year installer warranty.

Protection of openable windows to comply with NCC 2022 Volume Two, Part 3.9.2.5 and AS 1288; detailed design to be provided.

Surface water and stormwater drainage to comply with NCC 2022 Volume Two, Part 3.1.2 and AS/NZS 3500.3.

26 LUCINDA AVE, BASS HILL

CEDAR DESIGNS

IBRAHIM MUSTAPHA
BDAA ACCREDITED - 6450
BDAA MEMBER - 2360 - 17
REGISTERED DESIGN PRACTITIONER - DEP0000079

CEDAR DESIGNS PTY LTD
EMAIL: INFO@CEDARDESIGNS.COM.AU
WEBSITE: WWW.CEDARDESIGNS.COM.AU
PHONE: +61 410 289 126

ISSUE	DESCRIPTION
A	ISSUED FOR CLIENT REVIEW

Scale: 1 : 100 @ A2


CROSS SECTIONS + BASIX DETAILS

12/28


GENERAL NOTES
- Do not scale drawings, use figured dimensions only.
- All dimensions and levels are to be verified on site before any work commences.
- All work is to be carried out in accordance with the AS and NCC standards.

COPYRIGHT:
This document is COPYRIGHT and the property of CEDAR DESIGNS PTY LTD. It is not to be retained, copied or used without the prior written permission of CEDAR DESIGNS PTY LTD.

17/08/2026 5:20:43 PM

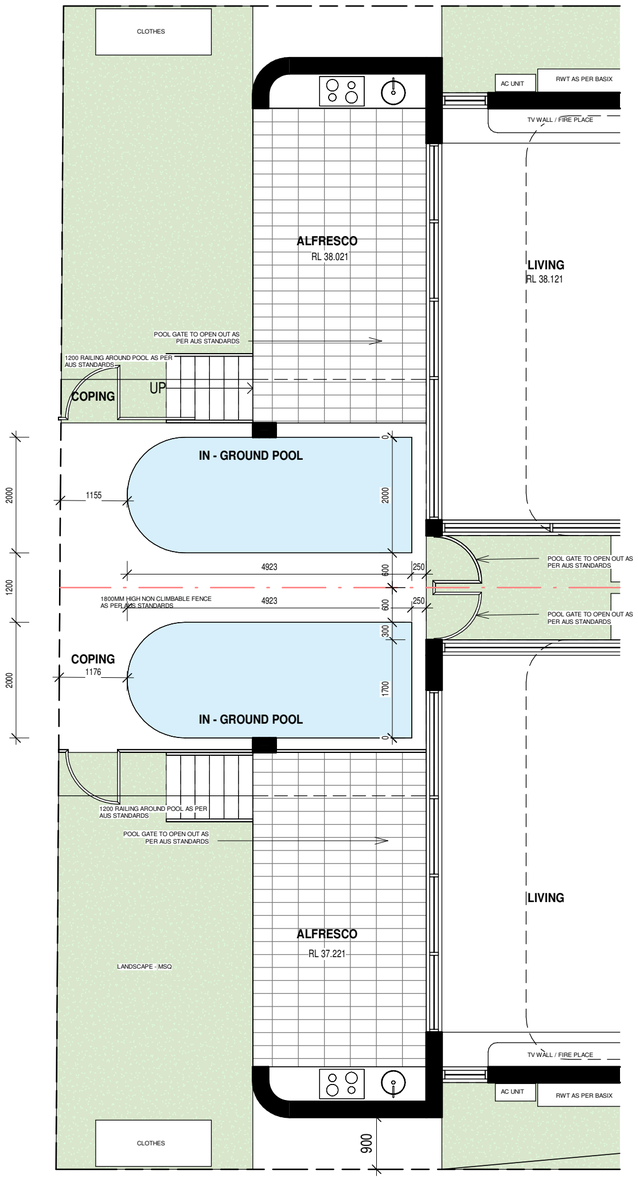

POOL PLANS
1 : 75

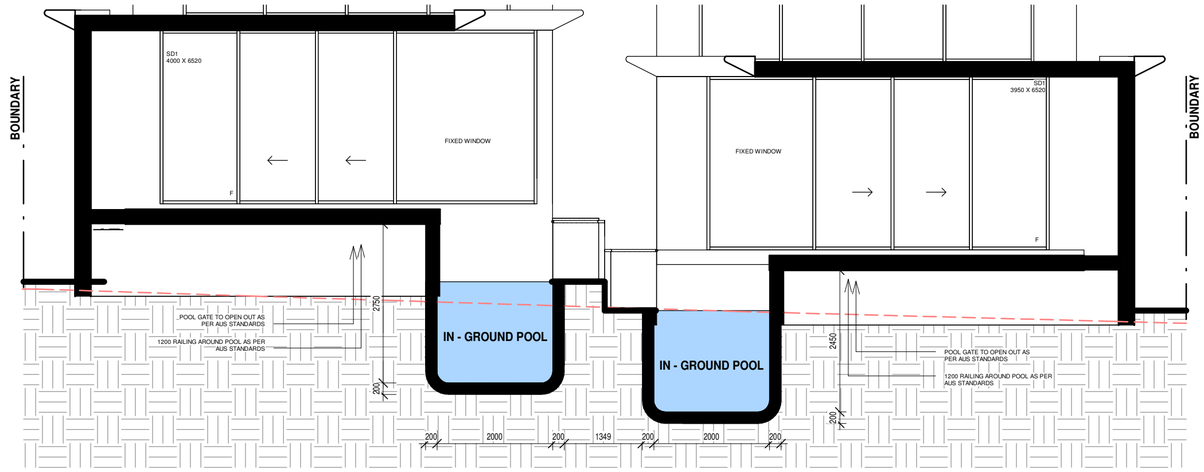

POOL SECTION
1 : 75

CALCULATIONS

POOL / SPA VOLUME CALCULATIONS	
	KILOLITRES
POOL	20
SPA	-

POOL TO BE CONSTRUCTED AS PER DETAILS AND SPECIFICATIONS OF A STRUCTURAL ENGINEER

POOL TO BE CONSTRUCTED COMPLYING WITH ALL THE AUSTRALIAN STANDARDS.

NOTES

COMPLIANCE WITH THE DCP / LEP or SEEP CONTROLS

1. SWIMMING POOL IS LOCATED IN THE REAR OF THE PROPERTY,

2. POOL TO BE LOCATED A MINUMUM OF 1000mm OF THE BOUNDARY.

3. THE POOL HAS BEEN DESIGNED TO BE AS CLOSE AS POSSIBLE TO THE EXISTING GROUND LEVEL, AS SHOWING IN THE CROSS SECTION.

4. NO PART OF THE SWIMMING POOL GOES 1400 ABOVE THE EXISTING GROUND LEVEL.

COMPLIANCE WITH THE AUSTRALIAN STANDARDS

1. THE POOL IS SEPARATED BY A COMPLYING BARRIER FROM THE HOUSE AND ADJOINING PROPERTIES.

2. THERE WILL BE NO DIRECT ACCESS TO THE POOL FROM THE HOUSE.


3. FENCE AROUND THE POOL WILL BE A MINIMUM OF 1200MM HIGH.

4. THERE WILL BE NO CLIMBABLE ZONES SURROUNDING THE POOL OR THE POOL BARRIER.

5. POOL FENCE WILL FRAMELESS GLASS FIXED TO THE GROUND, IF ANOTHER TYPE OF BARRIER IS SELECTED DURING CONSTRUCTION IT SHALL COMPLY WITH THE FOLLOWING:
- VERTICAL GAPS IN THE FENCE WILL NOT BE MORE THAN 100MM
- THE GAP AT THE BOTTOM OF THE FENCE WILL BE A MAXIMUM OF 100MM

6. POOL GATE WILL BE FITTED WITH A SELF CLOSING DEVICE, AND GATE WILL ONLY SWING OUT AWAY FROM THE POOL AREA.

7. GLAZING AROUND THE POOL AREA WILL BE FIXED GLAZING

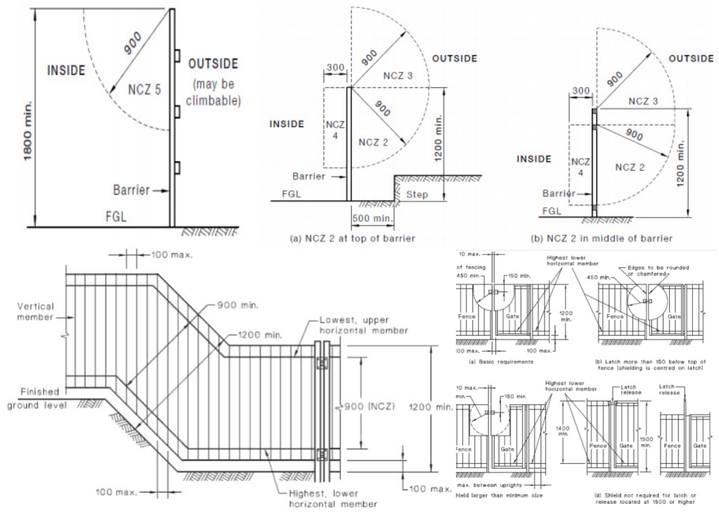

26 LUCINDA AVE, BASS HILL

CEDAR DESIGNS

IBRAHIM MUSTAPHA
BDAA ACCREDITED - 6450
BDAA MEMBER - 2360 - 17
REGISTERED DESIGN PRACTITIONER - DEP0000079

CEDAR DESIGNS PTY LTD
EMAIL: INFO@CEDARDESIGNS.COM.AU
WEBSITE: WWW.CEDARDESIGNS.COM.AU
PHONE: +61 410 289 126

ISSUE	DESCRIPTION
A	ISSUED FOR CLIENT REVIEW

Scale: 1 : 75 @ A2 | POOL PLANS 1 | 13/28

GENERAL NOTES
- Do not scale drawings, use figured dimensions only.
- All dimensions and levels are to be verified on site before any work commences.
- All work is to be carried out in accordance with the AS and NCC standards.

COPYRIGHT:
This document is COPYRIGHT and the property of CEDAR DESIGNS PTY LTD. It is not to be retained, copied or used without the prior written permission of CEDAR DESIGNS PTY LTD.

17/08/2026 5:20:44 PM



THERE MUST BE APPROPRIATE SIGNS INSTALLED ON SITE INCLUDING DETAILS OF CPR TECHNIQUES IN THE IMMEDIATE VICINITY OF THE POOL.

POOL TO BE CONSTRUCTED AS PER DETAILS AND SPECIFICATIONS OF A STRUCTURAL ENGINEER


POOL TO BE CONSTRUCTED COMPLYING WITH ALL THE AUSTRALIAN STANDARDS.


POOL FENCE REQUIRED IN ACCRDANCE WITH AS1926.1-2012


CALCULATIONS


POOL / SPA VOLUME CALCULATIONS

	KILOLITRES
POOL	20
SPA	-

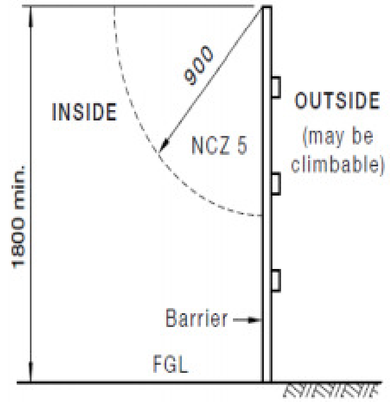

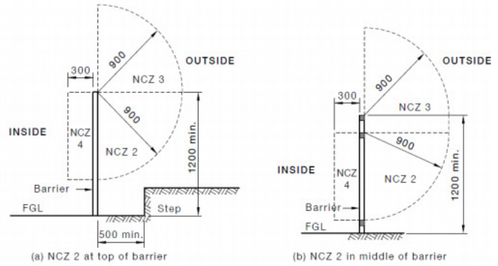

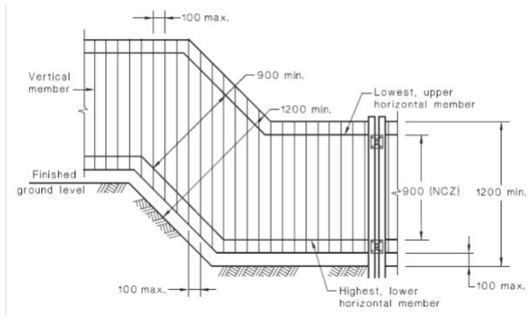

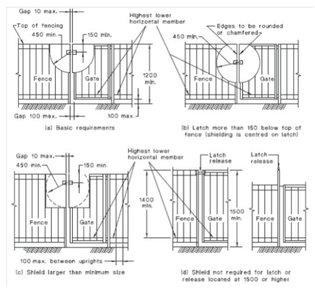

NOTES

COMPLIANCE WITH THE DCP / LEP or SEEP CONTROLS

1. SWIMMING POOL IS LOCATED IN THE REAR OF THE PROPERTY, BEHIND THE BUILDING LINE

2. POOL TO BE LOCATED A MINUMUM OF 1000mm OF THE BOUNDARY.

3. THE POOL HAS BEEN DESIGNED TO BE AS CLOSE AS POSSIBLE TO THE EXISTING GROUND LEVEL, AS SHOWING IN THE CROSS SECTION.

4. NO PART OF THE SWIMMING POOL GOES 1400 ABOVE THE EXISTING GROUND LEVEL.

COMPLIANCE WITH THE AUSTRALIAN STANDARDS

1. THE POOL IS SEPARATED BY A COMPLYING BARRIER FROM THE HOUSE AND ADJOINING PROPERTIES.

2. THERE WILL BE NO DIRECT ACCESS TO THE POOL FROM THE HOUSE.

3. FENCE AROUND THE POOL WILL BE A MINIMUM OF 1200MM HIGH.

4. THERE WILL BE NO CLIMBABLE ZONES SURROUNDING THE POOL OR THE POOL BARRIER.

5. POOL FENCE WILL FRAMELESS GLASS FIXED TO THE GROUND, IF ANOTHER TYPE OF BARRIER IS SELECTED DURING CONSTRUCTION IT SHALL COMPLY WITH THE FOLLOWING:
- VERTICAL GAPS IN THE FENCE WILL NOT BE MORE THAN 100MM
- THE GAP AT THE BOTTOM OF THE FENCE WILL BE A MAXIMUM OF 100MM

6. POOL GATE WILL BE FITTED WITH A SELF CLOSING DEVICE, AND GATE WILL ONLY SWING OUT AWAY FROM THE POOL AREA.

7. GLAZING AROUND THE POOL AREA WILL BE FIXED GLAZING

26 LUCINDA AVE, BASS HILL

CEDAR DESIGNS

IBRAHIM MUSTAPHA
BDAA ACCREDITED - 6450
BDAA MEMBER - 2360 - 17
REGISTERED DESIGN PRACTITIONER - DEP0000079

CEDAR DESIGNS PTY LTD
EMAIL: INFO@CEDARDESIGNS.COM.AU
WEBSITE: WWW.CEDARDESIGNS.COM.AU
PHONE: +61 410 289 126


ISSUE	DESCRIPTION
A	ISSUED FOR CLIENT REVIEW

Scale: @ A2 | POOL PLANS 2 | 14/28

GENERAL NOTES
- Do not scale drawings, use figured dimensions only.
- All dimensions and levels are to be verified on site before any work commences.
- All work is to be carried out in accordance with the AS and NCC standards.

COPYRIGHT:
This document is COPYRIGHT and the property of CEDAR DESIGNS PTY LTD. It is not to be retained, copied or used without the prior written permission of CEDAR DESIGNS PTY LTD.


17/08/2026 5:20:44 PM

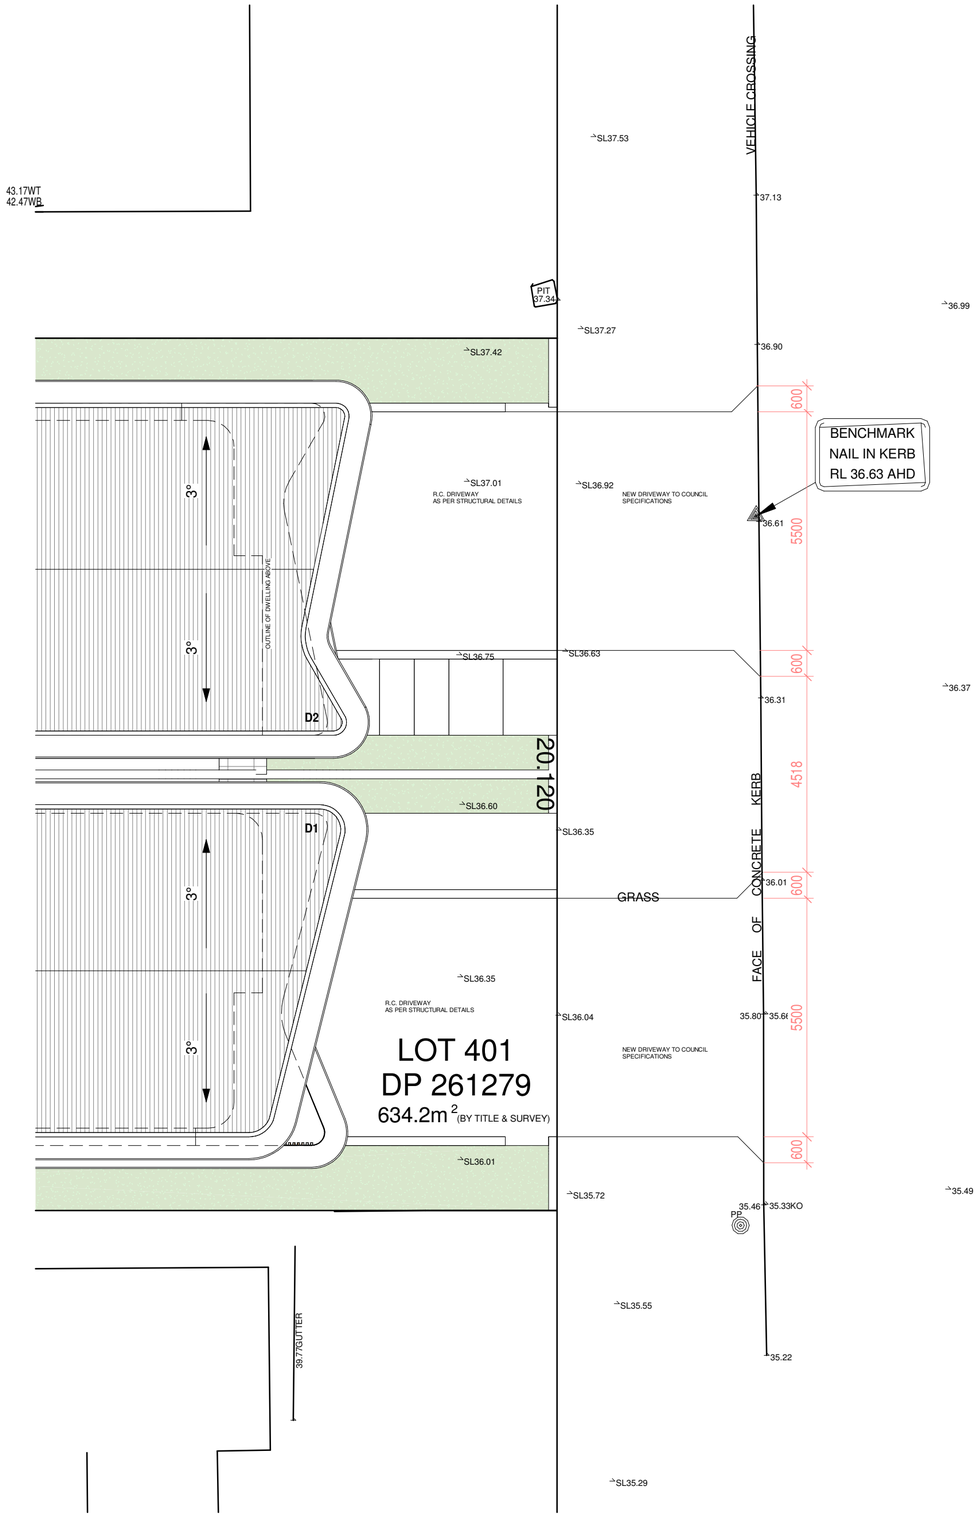


AVENUE

LUCINDA

DRIVEWAY PLAN
1 : 100

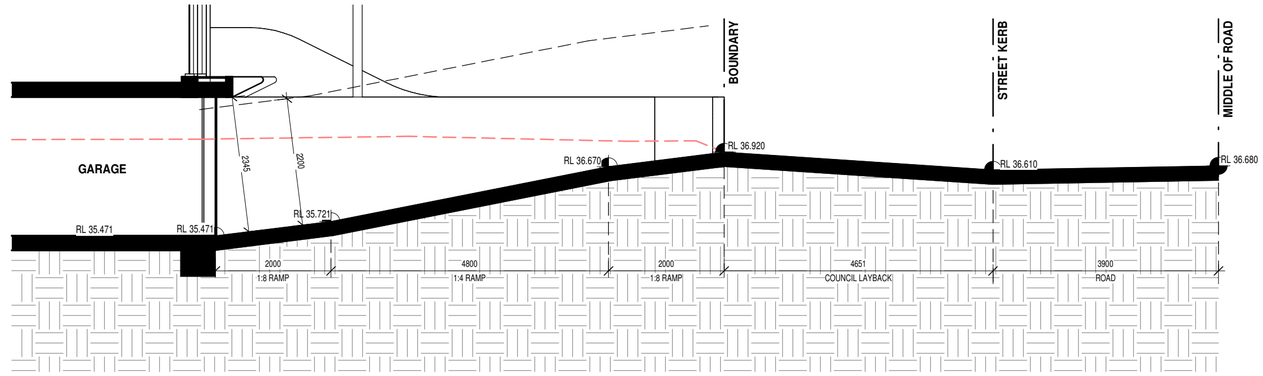

DWELLING 1 DRIVEWAY PROFILE
1 : 75

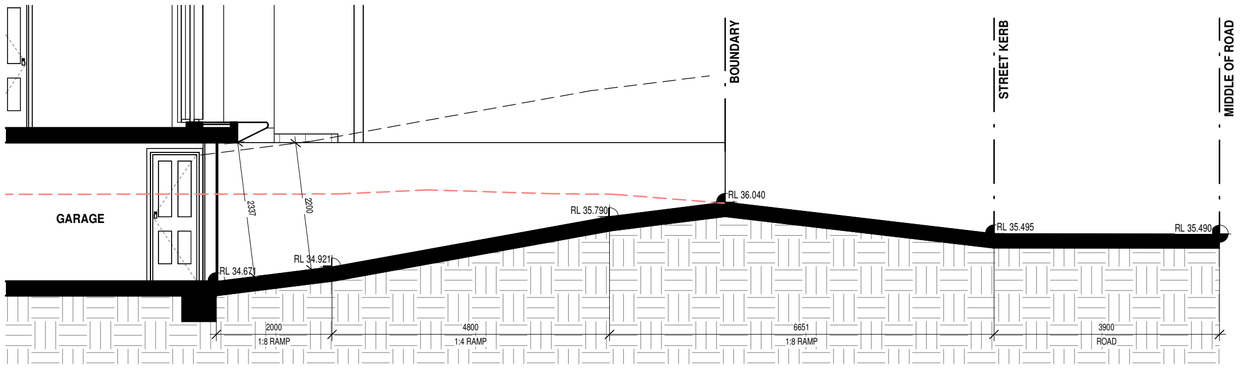

DWELLING 2 DRIVEWAY PROFILE
1 : 75

CONCEPT PLAN ONLY
NOT FOR CONSTRUCTION

ALL WORK TO COMPLY WITH AUS STANDARD 2890.1

PRIOR TO WORKS, A DRIVEWAY APPLICATION AND WORK PERMIT MUST BE OBTAINED FROM -

26 LUCINDA AVE, BASS HILL

CEDAR DESIGNS

IBRAHIM MUSTAPHA
BDAA ACCREDITED - 6450
BDAA MEMBER - 2360 - 17
REGISTERED DESIGN PRACTITIONER - DEP0000079

CEDAR DESIGNS PTY LTD
EMAIL: INFO@CEDARDESIGNS.COM.AU
WEBSITE: WWW.CEDARDESIGNS.COM.AU
PHONE: +61 410 289 126

ISSUE	DESCRIPTION
A	ISSUED FOR CLIENT REVIEW

Scale: As indicated @ A2

PROPOSED DRIVEWAY

17/28

GENERAL NOTES
- Do not scale drawings, use figured dimensions only.
- All dimensions and levels are to be verified on site before any work commences.
- All work is to be carried out in accordance with the AS and NCC standards.

COPYRIGHT:
This document is COPYRIGHT and the property of CEDAR DESIGNS PTY LTD. It is not to be retained, copied or used without the prior written permission of CEDAR DESIGNS PTY LTD.

17/08/2026 5:20:45 PM

FINISHES BOARD



FRONT GATES ON DRIVEWAY AND ENTRY
ALUMINUM
WHITE COLOUR




SELECTED TIMBER CLAD
TERRITORY WOODLANDS, EBONY
SUPPLIED BY CEMINTEL.





SELECTED RENDERE COLOUR OPTIONS
Natural White
Whisper White
White on White
Lexicon

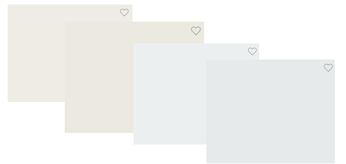

DRIVEWAYS, AND ENTRY PATHS
POLISHED CONCRETE - NON SLIP



FRONT DOOR:
SOLID TIMBER OR SIMILAR





GARAGE DOOR:
SEAMLESS TIMBER DOOR DECO WOOD OR SIMILAR



26 LUCINDA AVE, BASS HILL

CEDAR DESIGNS

IBRAHIM MUSTAPHA
BDAA ACCREDITED - 6450
BDAA MEMBER - 2360 - 17
REGISTERED DESIGN PRACTITIONER - DEP0000079

CEDAR DESIGNS PTY LTD
EMAIL: INFO@CEDARDESIGNS.COM.AU
WEBSITE: WWW.CEDARDESIGNS.COM.AU
PHONE: +61 410 289 126

ISSUE	DESCRIPTION
A	ISSUED FOR CLIENT REVIEW

Scale: @ A2

COLOURS AND FINISHES

20/28

GENERAL NOTES
- Do not scale drawings, use figured dimensions only.
- All dimensions and levels are to be verified on site before any work commences.
- All work is to be carried out in accordance with the AS and NCC standards.

COPYRIGHT:
This document is COPYRIGHT and the property of CEDAR DESIGNS PTY LTD. It is not to be retained, copied or used without the prior written permission of CEDAR DESIGNS PTY LTD.

17/08/2026 5:20:45 PM



26 LUCINDA AVE, BASS HILL

CEDAR DESIGNS

IBRAHIM MUSTAPHA
BDAA ACCREDITED - 6450
BDAA MEMBER - 2560 - 17
REGISTERED DESIGN PRACTITIONER - DEP0000079

CEDAR DESIGNS PTY LTD
EMAIL: INFO@CEDARDESIGNS.COM.AU
WEBSITE: WWW.CEDARDESIGNS.COM.AU
PHONE: +61 410 389 126

ISSUE	DESCRIPTION
A	ISSUED FOR CLIENT REVIEW

Scale: @ A2


3D PERSPECTIVE 1

21/28

GENERAL NOTES
- Do not scale drawings, use figured dimensions only.
- All dimensions and levels are to be verified on site before any work commences.
- All work is to be carried out in accordance with the AS and NCC standards.

COPYRIGHT:
This document is COPYRIGHT and the property of CEDAR DESIGNS PTY LTD. It is not to be retained, copied or used without the prior written permission of CEDAR DESIGNS PTY LTD.

17/08/2026 5:20:45 PM

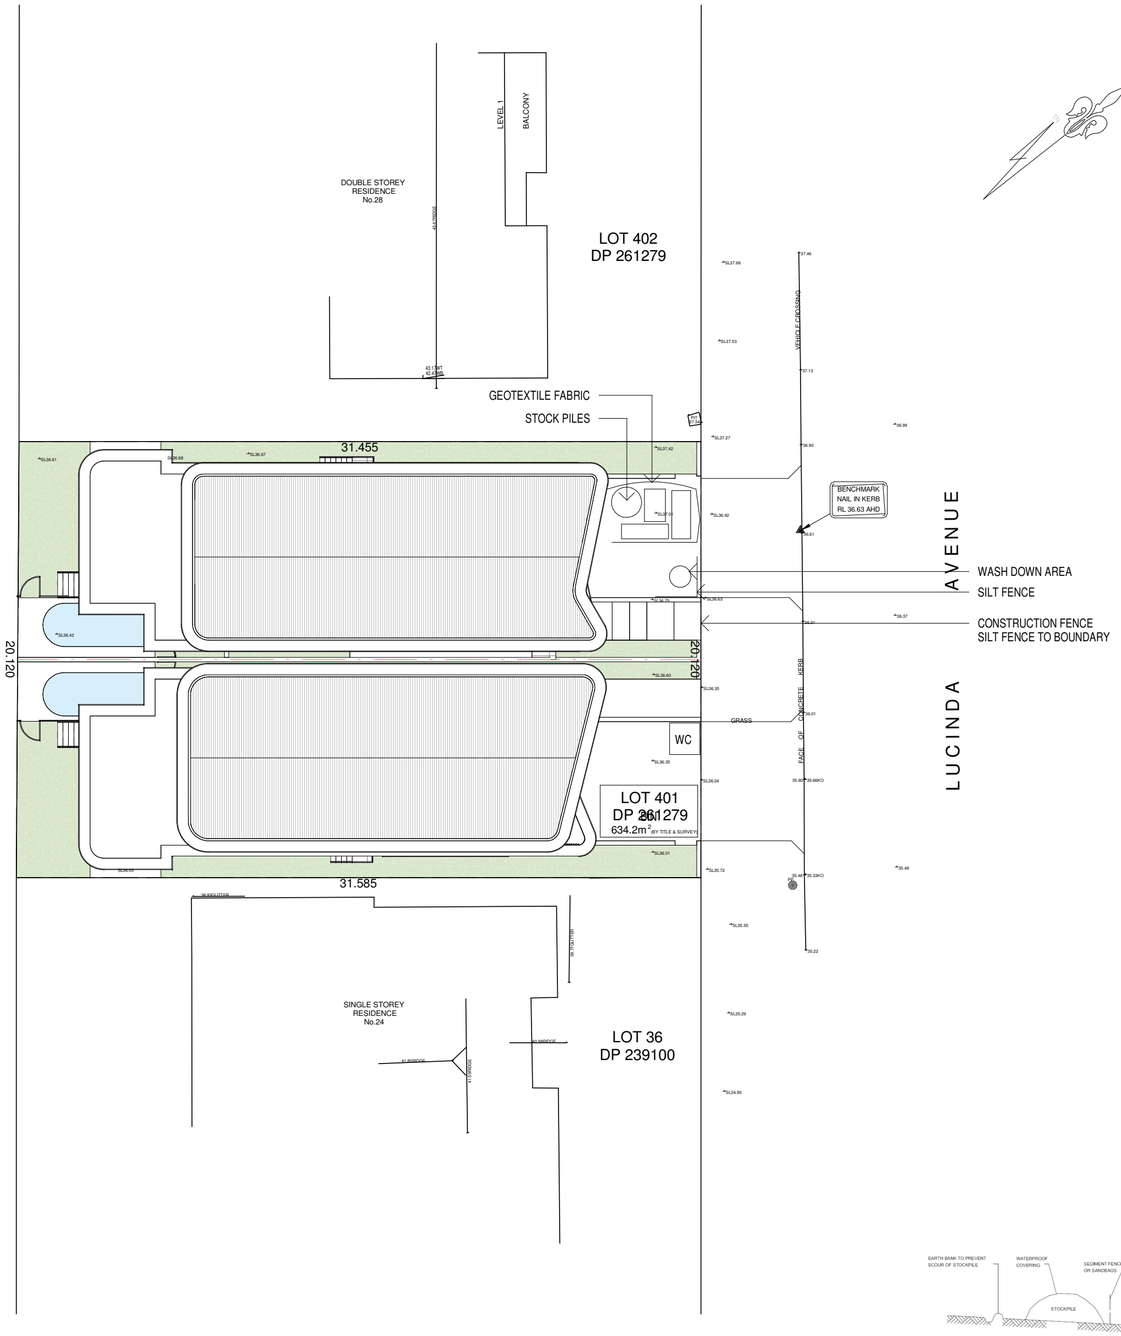

SILTATION MANAGEMENT PROCEDURE

1. Erect silt fence and gravel drain
2. Demolish existing structures
3. Excavate strip footings, according to enginners details.
4. Finish construction
5. Finish landscaping.
6. Silt fences are not to be removed until all construction and vegatation has been completed.


EROSION CONTROL NOTES

1. All erosion and sediment control measures to be installed prior to any site disturbance.
2. All control measure to be inspected and maintained daily by site manager.
3. Stripping of grass and other vegetation shall be kept to a minimum.
4. Topsoil from all areas that will be that will be disturbed to be stripped and stockpiled, and to be kept clear from gutters, drains, stormwater, and footpaths.
5. Drainage to be connected to storm water as soon as possible.
6. Road and footpath to be kept clean, and must be swept daily.
7. All sediment control structures must be inspected after rainfall for any structural damage, all trapped sediment will be removed to a nominated stockpile.


EROSION AND SEDIMENT CONTROL PLAN

1 : 200


WARNING: $4000 FINE
IT IS ILLEGAL TO ALLOW SOIL, CEMENT, OR ANY OTHER BUILDING MATERIAL TO BE DRAINED, PUMPED OR ALLOWED TO ENTER THE STORM WATER SYSTEM.

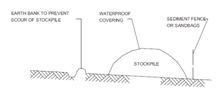


BUILDING MATERIAL STOCKPILES
NTS

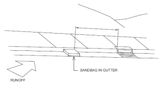


SANDBAG KERB SEDIMENT TRAP
NTS

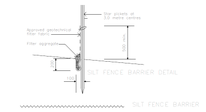

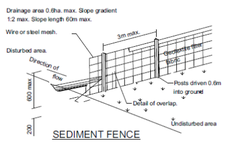

SEDIMENT FENCE

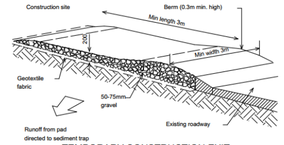

TEMPORARY CONSTRUCTION EXIT

26 LUCINDA AVE, BASS HILL

CEDAR DESIGNS

IBRAHIM MUSTAPHA
BDAA ACCREDITED - 6450
BDAA MEMBER - 2360 - 17
REGISTERED DESIGN PRACTITIONER - DEP0000079

CEDAR DESIGNS PTY LTD
EMAIL: INFO@CEDARDESIGNS.COM.AU
WEBSITE: WWW.CEDARDESIGNS.COM.AU
PHONE: +61 410 289 126

ISSUE	DESCRIPTION
A	ISSUED FOR CLIENT REVIEW

Scale: 1 : 200 @ A2


EROSION AND SEDIMENT CONTROL

25/28

GENERAL NOTES
- Do not scale drawings, use figured dimensions only.
- All dimensions and levels are to be verified on site before any work commences.
- All work is to be carried out in accordance with the AS and NCC standards.

COPYRIGHT:
This document is COPYRIGHT and the property of CEDAR DESIGNS PTY LTD. It is not to be retained, copied or used without the prior written permission of CEDAR DESIGNS PTY LTD.

17/08/2026 5:20:46 PM

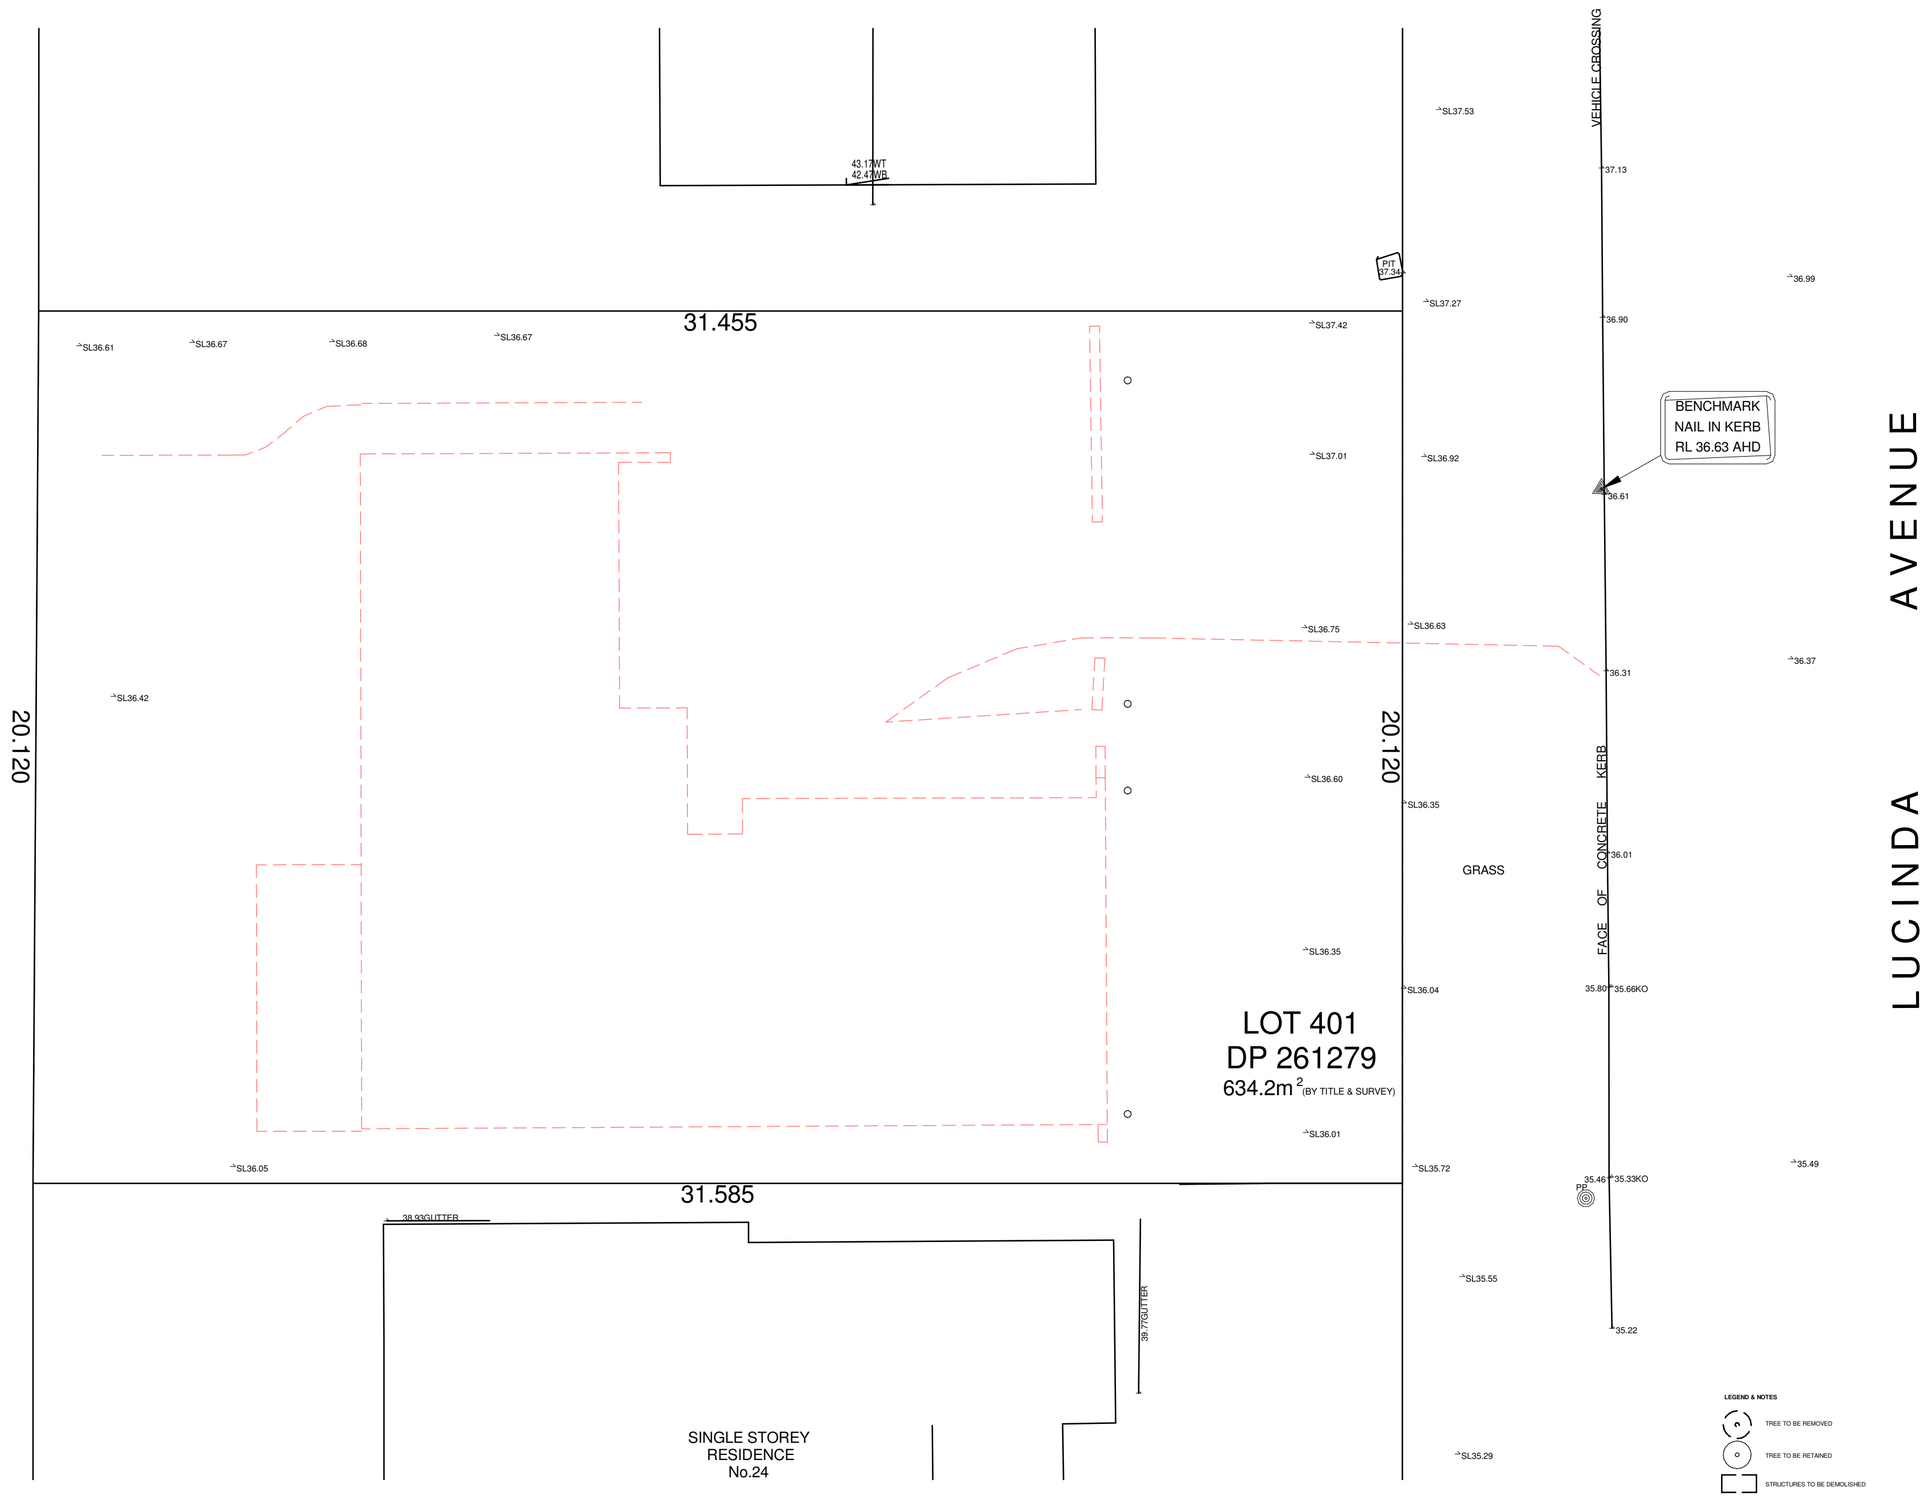

DEMOLITION PLAN

1 : 100

All demolition work shall be carried out in accordance with AS2601 — 2001: The Demolition of Structures and with the requirements of the WorkCover Authority of NSW.

26 LUCINDA AVE, BASS HILL

CEDAR DESIGN

IBRAHIM MUSTAPHA
BDAA ACCREDITED - 6450
BDAA MEMBER - 2360 - 17
REGISTERED DESIGN PRACTITIONER - DEP0000079

CEDAR DESIGNS PTY LTD
EMAIL: INFO@CEDARDESIGNS.COM.AU
WEBSITE: WWW.CEDARDESIGNS.COM.AU
PHONE: +61 410 289 126

ISSUE	DESCRIPTION
A	ISSUED FOR CLIENT REVIEW

Scale: As indicated @ A2

PROPOSED DEMOLITION PLAN

26/28

GENERAL NOTES
- Do not scale drawings, use figured dimensions only.
- All dimensions and levels are to be verified on site before any work commences.
- All work is to be carried out in accordance with the AS and NCC standards.

COPYRIGHT:
This document is COPYRIGHT and the property of CEDAR DESIGNS PTY LTD. It is not to be retained, copied or used without the prior written permission of CEDAR DESIGNS PTY LTD.

17/08/2026 5:20:46 PM

GENERAL

G1 - These drawing shall be read in conjunction with all other working drawings and specifications and with such other written instructions as maybe issued during the course of the construction. All discrepancies and variations shall be referred to the engineer before proceeding with the work.

G2 - All materials and workmanship shall be in accordance with the relevant and current standards Australia code and with the BY-LAWS and ordinances of the relevant building authorities except where varied by the project specification.

G3 - All dimensions shown shall be verified by the builder on site. Engineer's drawings shall not be scaled for dimensions. Engineer's drawings issued in any electronic format must not be used for dimensional setout.Refer to the architect's drawings for all dimensional setout information.

G4 - During construction, the structure shall be maintained in a stable condition and no part shall be overstressed. Temporary bracing shall be provided by the builder to keep the works and excavations stable at all times.

G5 - Unless noted, otherwise all levels are in meters and all dimensions are in millimeters.

FOOTING:

F1 - Footings shall be located centrally under wall and columns unless noted otherwise.

F2 - Do not backfill retaining walls (other than cantilever walls) until floor construction at top and bottom is completed. Ensure free draining backfill and drainage is in place.

F3 - Footings to be constructed and backfilled as soon as possible following excavation to avoid softening or drying out by exposure.

F4- Footing have been designed for allowable bearing pressure of Foundtaion materials shall be approved for this pressure before placing concrete in footings. NoteL Firm uniform natural bearing must be obtained.

SLAB MAINTENANCE

SM1 - During the life of a building, damage in various forms is likely to occur to the concrete slab. Good housekeeping will keep problems to a minimum and extend the life of the floor and road slabs. The following likely areas of damage may or may not occur during the life of the building.

SM2 - Damage to joints such as fretting or breaking away at floor should be repaired using epoxy concrete repair products and the jointing material made good.

SM3 - Cracking of slabs which may occur over the life of the slab should be repaired by epoxy grouting as soon as possible to prevent local fretting and breaking away. The definition of a crack which may become detrimental is one which is greater than 0.3mm.

SM4 - Local damage due to mechanical processes or pallets (with protruding nails) should be repaired as soon as possible with an epoxy concrete repair product.

SM5 - Local movement of slabs caused by external sources such as egress of water should be referred to the structural engineer to determine the best method of repair.

SM6 - Joint sealants will generally break down and need replacement after 12 months when most of the slab shrinkage has taken place. Resealing needs to be carried out to ensure ongoing support to slab edges.

SM7 - If solid wheeled materials handling equipment is to be used. Joint damage can be expected and a regular maintenance program will be required.

WELD TESTING

W1 - Testing of category SP welds shall be completed using ultrasonic testing methods by an approved testing authority in accordance with AS1554, Part 1-1985.

W2 - Minimum testing required shall be at least 50% of full strength butt welds.

W3 - Should any weld be found defective in accordance with AS1554:1 1985 further tests shall be carried out on the same steel work to compliance as shown.

W4 - All defective welds shall be ground out.

TIMBER

T1 - All material and workmanship shall be in accordance with AS1720. Timber sized where not indicated shall be in accordance with AS1684 or NSW timber framing manual.

T2 - Timber sizes quoted are nominal, actual sizes shall not be more than 5% under quoted sizes.

T3 - Timber particle-board flooring shall be 19mm thick premium grade to AS1859 and shall be laid strictly in accordance with the manufacturers details and specifications.

T4 - All roof trusses and rafters shall be fixed to wall plates using 2 'Teco Triple Grip' connectors at each joint.

CONCRETE

C1 - All workmanship and materials shall be in accordance with AS3600 except as varies by the contract documents.

C2 - Readymix Concrete supply shall comply with AS1379

C3 - Concrete components and quality shall be as follows:

Building Elements Footing & Slab	Footing & Slab on Ground	Suspended Cone & Cols F'c
F'c MPa	25	32
Max.agg.size mm	20	20
Slump mm	60-100	80-100
Cement type	A	A
Admixture	NIL	NIL
Control Testing Type	PLANT	PLANT

All concrete strength must be verified by plant testing unless otherwise specified.

C4 - Clear concrete cover to reinforcement including ties and stirrups shall be as follows in the table below unless otherwise:minimum cover to reinforcement to comply with exposure and /or 90min.fire-resistance

Structural Element	Concrete Strength (MPa)	Condition A1 in sheltered location or protected by approved W.P.M	Condition A2 exposed to non-aggressive soil & non-industrial & cost line>50km	Condition B1 1 to 50kms from coastline, exposed to environment & industrial	Condition B2 under 1km from coastline & exposed environment
Pads, Footing, Pile & Pile cape	20	---	65	75	---
	25	---	50	65	---
	32	---	40	50	60
	40	---	30	40	50
Strip footing and pedestals	20	---	50	---	---
	25	---	40	60	---
	32	---	30	40	65
	40	---	20	30	45
Columns	20	---	---	---	---
	25	25	30	---	---
	32	25	25	40	---
	40	25	25	30	45
Beams	20	---	---	---	---
	25	30	30	---	---
	32	30	25	40	---
	40	30	25	30	45
Slabs	20	30	50	---	---
	25	30	30	---	---
	32	25	25	40	---
	40	25	25	30	45
Walls	20	35	50	---	---
	25	35	35	---	---
	32	35	35	40	---
	40	35	35	35	45

Where concrete is casting against the ground in the nonresidential construction, the cover given in the table above shall be increased by 20mm to the surface in contact with the ground or 10mm if that surface is protected by a damp-proof membrane. Chairs for reinforcement shall be obtained by the use of stainless steel or plastic bar chairs for bottom reinforcement. All chairs to be spaced at maximum of 750mm centers

C5 - Construction joints shall be properly formed and used only where shown or specifically approved by the engineer.

C6 - No holes, chases or embedment of pipes, other than those shown on the structural drawings shall be made in concrete members without the prior approval of the engineer.

C7 - Where the lap length is not specified, it shall be sufficient to develop the full strength of the reinforcement and not less than shown in the table below:

Combination of minimum values		Minimum tensile development length of reinforcement splices in mm for standard compaction and formwork to AS3600&AS3610						
Concrete Strength	Cover to nearest bar or fitment	Reinforcement Bar Sizes						
		N12	N16	N20	N24	N28	N32	N36
20MPa 25MPa 32MPa	50mm 30mm 25mm	375	475	700	950	1250	1550	1875
25MPa 32MPa 40MPa	60mm 40mm 30mm	300	400	550	750	1000	1225	1500
32MPa 40MPa 50MPa	65mm 45mm 35mm	300	400	500	600	800	1000	1200
40MPa 50MPa	70mm 50mm	300	400	500	600	700	800	950

C8 - All reinforcement shall be to AS1302 symbols:
F: wire reinforcing fabric R: Structural grade round bar
N: Deformed bars W: Plain & deformed bar
Designation code of reinforcement bars as in example: 17N20@350
17: no. of bars in groups 350: Spacing in mm ctc.
N20: nominal bar size in mm

C9 - Horizontal formwork shall be stripped when approved by the engineer.

C10 - Splices in reinforcement shall be made only in the position shown or as otherwise approved by the engineer.

C11 - All concrete shall be placed and 'cured' in accordance with AS3600. Where curing compound is used it must be applied:
(a) Onto slab within 2 hours of placing concrete
(b) Onto walls and columns immediately after stripping the formwork

C12 - Slabs and beams shall bear only on the beams, walls, etc., shown on the drawings; all other building elements shall be kept 15mm clear from soffits of structure. All reinforcement shall be to AS1302 symbols: E: wire reinforcing fabric.

C13 - Removal of formwork and formwork supports from under the slabs and beams not supporting structures above and not carrying superimposed construction loads greater than 1.5kPa shall be done to the following guidelines:

Formed Surface	Classification of the supporting member	Hot condition t>21°C	Average condition 12°C<t<21°C	cold condition t>5°C
Beams	Forms supports for eff span	5 days	7 days	12 days
	<3m	10 days	21 days	28 days
	3-5m	14 days	21 days	28 days
	>5m	14 days	28 days	28 days
Slabs	Forms supports for eff span	4 days	6 days	8 days
	<3m	7 days	14 days	21 days
	3-5m	10 days	21 days	28 days
	>5m	14 days	28 days	28 days
Walls	Forms	5 days	7 days	9 days

C14 - Reinforcement is shown diagrammatically: it is not necessarily shown in true projection

C15 - Slab reinforcement shall extend at least 65mm onto masonry support walls unless notedotherwise

C16 - Where TRANSVERSE BARS are not shown provide N12@400 splice where necessary and lap with main bars: 400mm

C17 - Columns, piers and pedestals shall be placed 48 hours minimum prior to concrete placing in the slabs and beams above.

C18 - Curing of all concrete surfaces shall commence immediately after surfaces finished as specified.

C19 - Concrete sizes do not include thickness of applied finishes

C20 - Depths of beams are given first and include slab thickness


C21 - Refer to architect's details for chamfers, drip grooves, reglets, etc., maintain cover to reinforcement at these details.

C22 - Standard cog lengths unless noted otherwise:

Bar Diameter	Min Cog Length (mm)
N12	180
N16	210
N20	260
N24	310
N28	360
N32	400

NOTE: Increase bar laps by 30% where concrete depth below bar is more than 300mm

C23 - Minimum mesh laps:

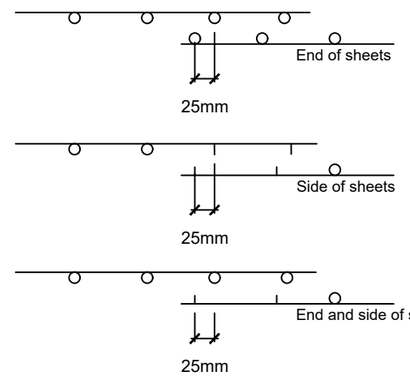

C27 - The engineer shall be given 24 hours notice for reinforcement inspection and concrete shall not be delivered until engineers approval is obtained

RK INFRA
DESIGN | CONSULTING | DEVELOPMENT

Designed/Drawn M.HOSNI
Approved K.NAJJAR
Checked A.ASHOSH
MOBILE 0414062484
Council CANTERBURY BANKSTOWN
Job No. 26LUC
Lot/DP 401/261279
PROJECT PROPOSED DUAL OCCUPANCY
Rev.No 02
Publish Date 18/08/2026
DRAWING TITLE GENERAL NOTES 1
26 LUCINDA AVENUE, BASS HILL, NSW
NTS
DRAWING NO. ST01

The contractor and / or subcontractors shall be responsible for all levels and dimensions prior to commencing on site or off site constructions and/or fabrications. These drawings must not be scaled. These drawings are dimensioned in (mms).These drawings must be read in conjunction with all other drawings and/or instructions as may be issued during the course of the project.These drawings are copyright and must not be retained, copied, developed or amended without a written consent from RK INFRA. All works resulting of these drawings are to be in accordance with 1- The Building Code of Australia. 2- All codes and regulations of LOCAL AUTHORITY REQUIREMENTS. 3- All related Trades Australian Standards. These drawings are site specific and can only be used for the address as listed in these drawings. These drawings are site specific and can only be used for the address listed in these drawings. 1. All works to be in accordance with the Building Code of Australia, Australian Standards, statutory regulations and local authority requirements. 2. Consistency between similar materials to be maintained. RK INFRA to be notified discrepancies, dimensional inconsistencies or the need for clarification prior to manufacture. 3. RK INFRA to approve all detailed drawings/setting out prior to construction.5. Contractors to confirm stability and feasibility of all units/components manufacture. 6. All drawing measurements to be verified on site - do not scale from documents. 7.Refer to this document in conjunction with Specification or any other plans such as structural, hydraulic and electrical (if applicable) for further information.

STRUCTURAL STEELWORK

S1 - All workmanship and materials shall be in accordance with AS4100, AS1554 and all other relevant documents & specification.

S2 - Hole punching will not be permitted in the material of base thickness greater than 10mm

S3 - Materials of thickness greater than 12mm must not be sheared unless approved by the engineer.

S4 - All welds shall be 6mm-E48XX-Category 'SP' continuous fillet or full penetration butt welds to AS1553, AS1554 and AS4100 unless noted otherwise.

S5 - All gusset plates shall be 10mm thick unless noted otherwise.

S6 - All bolts shall be M20-4.6 N/S unless noted otherwise.

S7 - All standard bolt holes shall be of diameter 2mm max. greater that of the bolt and of diameter 1mm max greater that of the pin or the high strength bolt.

S8 - All steelwork not encase in concrete shall be painted as follows:
- a- two 75mic. (DFT) coats of Dulux Zincanode 304 paint, or
- b- after completion or erection where site welds are used two additional on site coats, to effected areas, as per 'a'.

No paint shall be applied until the preparation work has been inspected and passed by the engineer unless noted otherwise

Application DFT must be inspected/passed by the engineer unless noted otherwise

Alternatively all steelwork not encase in concrete shall be hot dip galvanized to AS4680@min. coat thickness of 100mic

All paint work shall be applied to manufacturer's written specifications.

S9 - The paintwork specification shall be extended as follows:
one 125 mic. (DFT) coat of Dulus Dureblid STE followed by two 60mic.(DFT) full gloss coats of Dulux Acrathane IF, in selected color. Other paint system may be used with engineer's approval

S10 - Grouting for bases and base plates shall consist of a stiff non-shrink 25MPa epoxy mortar mix hammered into place unless noted otherwise.

S11 - All cold-formed or pressed sections of 2.6mm or thicker sections shall be formed of an approved galvanized materials.

BRICK AND BLOCK MASONRY


M1 - All workmanship & material shall be in accordance with AS3700-Masonry structures, current addition with amendments and manufacture's specifications where applicable.

M2 - The design strength of masonry shall be:


Masonry Elements	Unconf. Strength or f'uc	Mortar Composition		
		Cement	Lime	Sand
Load bearing brickwork	50MPa	1	0.25	3
Ground floor load bearing brickwork	50MPa	1	0.25	3
General brickwork	20MPa	1	1.00	4
Concrete Blockwork	20MPa	1	0	3

M3 - Wall ties shall be minimum grade 316 medium duty. Type A stainless steel wall ties to conform to AS3700 and AS2699-SAA Wall ties for Masonry Construction. Ties shall be spaced at 400*600 max ctrs unless noted otherwise.

M4 - Horizontal joints at concrete slab (unless detailed otherwise)

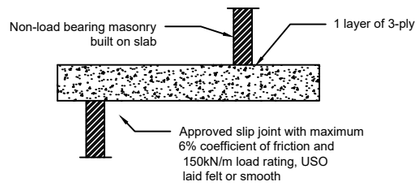

M4(b) - Non-load bearing masonry

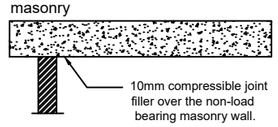

M5 - Damp-proof course material shall be at least 20mm wider than the thickness of the masonry in which it is placed.

M6 - Over-flashing, where applicable, shall be set into mortar joints raked to the depth of at least 15mm into masonry.

M7 - Vertical expansion joints shall be provided at 6m max centers U.N.O

M8 - Weep holes (or 10mm drainage tubes for grouted masonry) shall be provided at vertical joints spaced at 1000max. Start in the external masonry walls; open full height above the damp-proof course of flashing.

M9 - No chases shall be cut into load bearing masonry without the written approval of the structural engineer U.N.O

M10 - All cavities shall be left free from mortar droppings or other material which might bridge or block the cavity.

M11 - Freshly laid masonry shall not be used to support scaffolding, formwork or any other equipment.

M12 - Unless noted otherwise the cores or cavities of reinforced masonry shall be filled with concrete having a characteristic compressive strength at 28 days of 25MPa and complying to AS3600 with min.300kg/cu.m cement.

M13 - When place concrete (or grout) shall have a slump of 150-200mm and it shall be fully compacted.

M14 - Maximum coarse aggregate size in concrete used to fill cores or cavities shall not be greater than 10mm.

M15 - Minimum reinforced cover shall be 30mm to comply to AS3700 Classification R4 and the requirement for a fire-resistance period of 120min or as may be required by local council.

M16 - All reinforced block-work must be provided with the inspection and clean-out holes.

M17 - Flashing must provided at all cavity, along with weep holes or drainage outlets as per Clause 11 of these notes.

M18 - All load bearing brickwork and un-reinforced concrete masonry shall have galvanized woven wire mesh placed into mortar at every second horizontal joints to first 4 joints above the slab and where required by the standard specification and good building practices.

M19 - All reinforcement bars must be galvanized with min.coating mass 600g/sqm horizontal bars placed centrally, so as not to interfere with the placement of vertical reinforcement U.N.O

M20 - The splices should be located just above the footings so that the vertical reinforcement may be tied to starter bars through clean-out holes

M21 - All additional splices and clean-out holes should be placed at the intermediate heights, corresponding to the grouting brick.

M22 - All load bearing brickwork shall have a characteristic unconfined compressive strength of 30MPa as defined by AS3700 mortar type shall be 1:3 (Cement:Sand)

M23 - All wall cavity shall be filled with cement mortar from the top of the footing to below the damp course unless otherwise

M24 - Where brickwork supports concrete slab and beams top course shall be laid frogs down and covered with two layers of method similar.

STANDARD LINTELS FOR BRICKWORK

All lintels for brickwork shall be of the size as listed below U.N.O

SPAN(mm)	Standard Angle	Galinlet	SPAN (mm)	Standard Angle
a. Non-load bearing internal and external wall			b. All load bearing wall	
Upto 600mm	75*10 Flat Plate	85*85*5kg/m FLAT	Upto 600mm	75*10 Flat Plate
625-900	75*50*6L	100*100*9.5 kg/m L	625-900	75*75*8L
925-1200	75*50*6L	100*100*9.5 kg/m L	925-1200	100*75*8L
1225-1800	75*75*8L	100*100*9.5 kg/m L	1225-1800	125*75*10L
1825-2100	100*75*8L	100*100*9.5 kg/m L	1825-2100	150*90*10L
2125-2400	100*75*10L	150*100*12 kg/m L	2125-2400	150*90*10L
2425-2700	100*75*10L	150*100*12 kg/m L	2425-2700	150*90*12L
2725-3000	125*75*10L	N.A	2725-3000	250UB37 or 2-180UB22

NOTES TO THE TABLE:
1. This table is to be read in conjunction with structural steelwork notes.
2. Galintel is a proprietary lintel by Galinted pty.Ltd.
3.All lintels to have a minimum bearing length of 110mm each end and to be hot dip galvanized to AS4680

SITE PREPARATION

SP1 - Strip off all vegetation, rubbish and topsoil containing organic or root matter from the area of the building.

SP2 - Provide suitable surface and/or subsoil drainage in conjunction with, or subsequently, bulk earthwork as required on site, to minimize ingress of moisture adjacent to , or beneath the building

SP3 - Fill consisting of material compacted to 95% max. STD dry density in layers by repeated rolling with tracked excavator or proprietary compaction plant.

SP4 - Filling is to be free of rubbish, plastic clay or large pieces which would inhabit compaction.

SP5 - Rolled fill depth shall not exceed 0.6m compacted in layers no more than 300mm for sand material or 300mm compacted in layers of not more tha 150mm for other approved material.

SP6 - The fill shall continue past the edge of the slab by at least 1.0m and shall be retained or battered beyond this point by a slope protected from erosion and not steeper than two horizontal to one vertical.

SP7 - Blind with sand and lay vapor-proof membrane.

SP8 - Vapour barrier shall be polyethylene sheeting of 0.2mm thickness, lapping shall be not less than 200mm at joints. penetrations by pipes shall be taped.

SP9 - If fill exceeds 600mm from natural ground level for the slab on ground, provide extra bottom steel mesh or to be referred to engineer.

RK INFRA
DESIGN | CONSULTING | DEVELOPMENT

Designed/Drawn
M.HOSNI

Approved
K.NAJJAR

Checked
A.ASHOSH

MOBILE
0414062484

Council
CANTERBURY BANKSTOWN

Job No.
26LUC

Lot/DP
401/261279

PROJECT
PROPOSED DUAL OCCUPANCY

Rev.No
02

Publish Date
18/08/2026


DRAWING TITLE
GENERAL NOTES 2

26 LUCINDA AVENUE, BASS HILL, NSW

NTS

DRAWING NO.
ST02

The contractor and / or subcontractors shall be responsible for all levels and dimensions prior to commencing on site or off site constructions and/or fabrications. These drawings must not be scaled. These drawings are dimensioned in (mms).These drawings must be read in conjunction with all other drawings and/or instructions as may be issued during the course of the project.These drawings are copyright and must not be retained, copied, developed or amended without a written consent from RK INFRA. All works resulting of these drawings are to be in accordance with 1- The Building Code of Australia. 2- All codes and regulations of LOCAL AUTHORITY REQUIREMENTS. 3- All related Trades Australian Standards. These drawings are site specific and can only be used for the address as listed in these drawings. These drawings are site specific and can only be used for the address listed in these drawings. 1. All works to be in accordance with the Building Code of Australia, Australian Standards, statutory regulations and local authority requirements. 2. Consistency between similar materials to be maintained. RK INFRA to be notified discrepancies, dimensional inconsistencies or the need for clarification prior to manufacture. 3. RK INFRA to approve all detailed drawings/setting out prior to construction.5. Contractors to confirm stability and feasibility of all units/components manufacture. 6. All drawing measurements to be verified on site - do not scale from documents. 7.Refer to this document in conjunction with Specification or any other plans such as structural, hydraulic and electrical (if applicable) for further information.

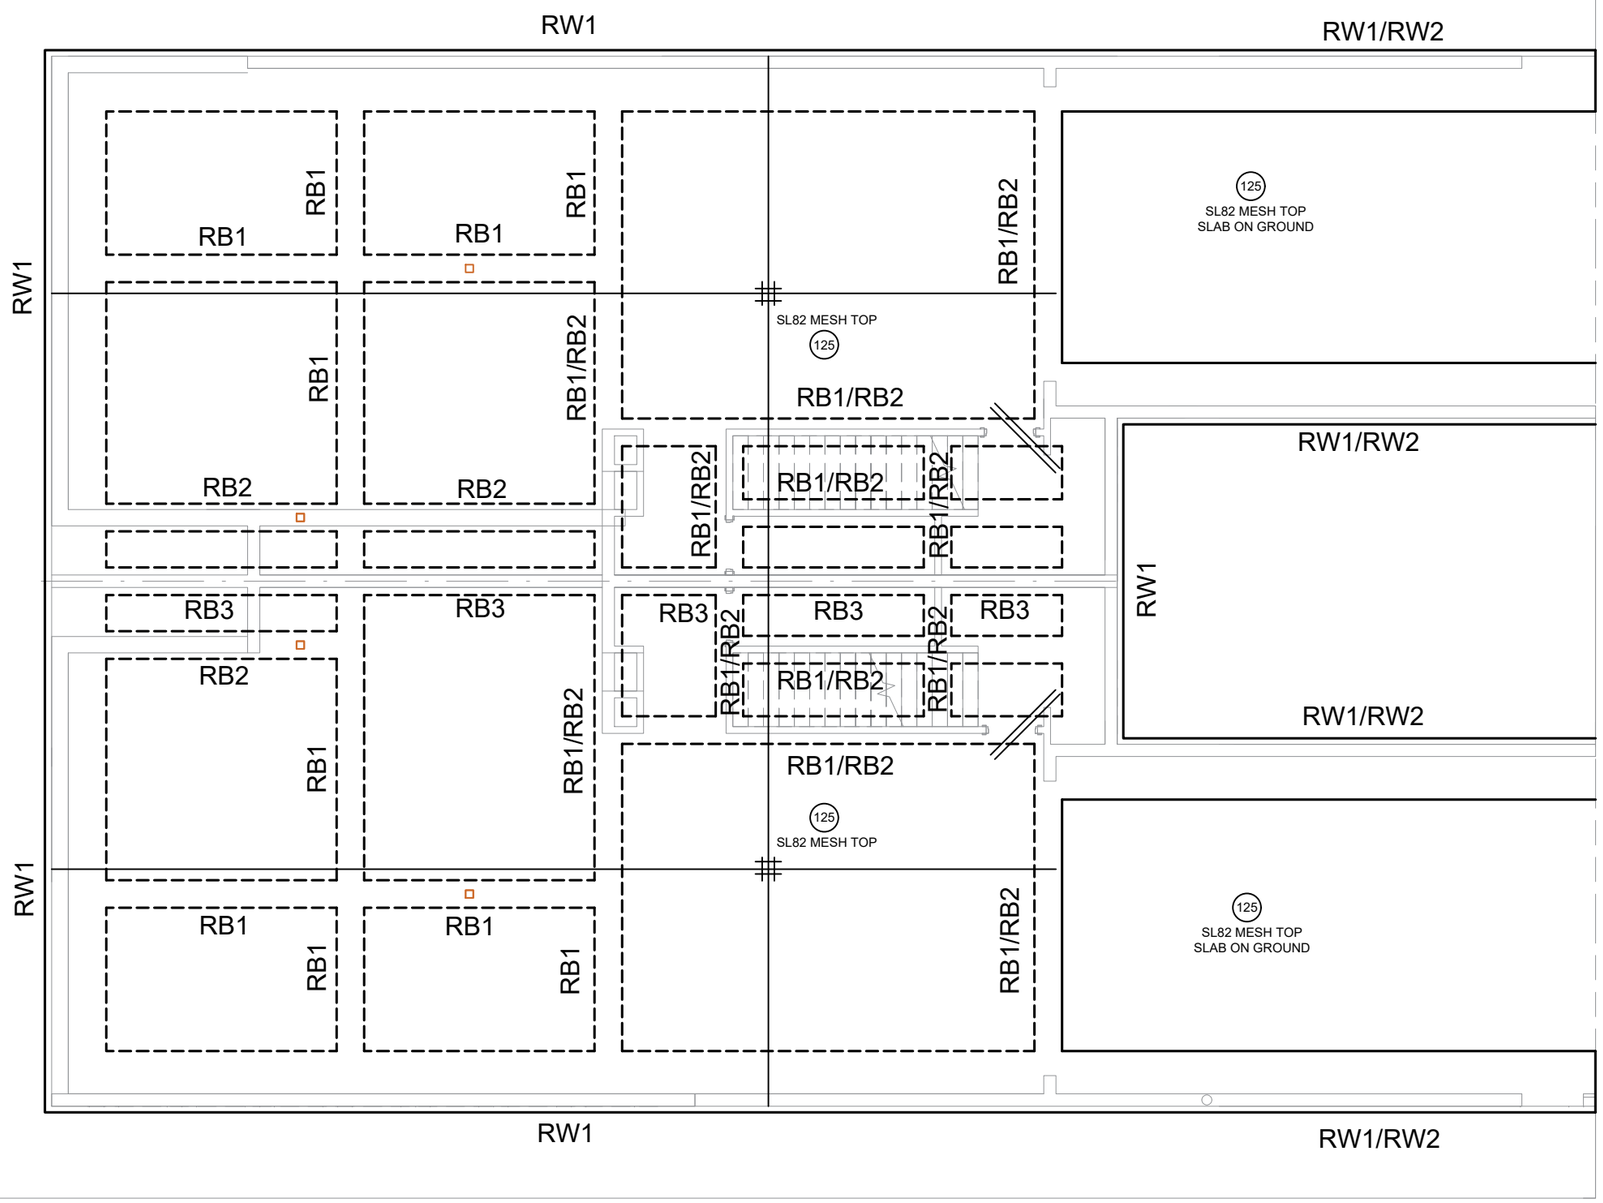

CONCRETE SLAB LAYOUT

SCALE 1:100

(125) DENOTES SLAB THICKNESS

- SLAB LEVEL TO BE TAKEN FROM ARCHITECTURAL PLANS.
- SLAB REINFORCEMENT TO BE SL82 MESH TOP UNLESS DENOTED ON LAYOUT.
- MIN. SLAB COVER TO BE 25mm TOP.
- MIN. FOOTING COVER TO BE 40mm.
- CONCRETE STRENGTH (fc) = 32MPa.

TR DENOTES 2N12 TRIMMERS BARS TOP EXTENDING 600 PAST CORNERS. (1500mm MIN. LENGTH).

LEGEND	
RB1	CONCRETE BEAM. REFER TO DETAILS
RW1	RETAINING WALL. REFER TO DETAILS
RB2	CONCRETE BEAM. REFER TO DETAILS
RB3	CONCRETE BEAM. REFER TO DETAILS
RW2	RETAINING WALL. REFER TO DETAILS

NOTE FOR FOUNDATIONS:

IF BASEMENT FOUNDATIONS ARE FOUNDED IN ROCK OR SHALE LAYER, PROVIDE 200mm THICK SLAB ON GROUND WITH SL92 TOP & BTM. RB1 & RB2 CAN BE REMOVED.

CONTACT ENGINEER IF REQUIRED.

RK INFRA
DESIGN | CONSULTING | DEVELOPMENT

Designed/Drawn
M.HOSNI

Approved
K.NAJJAR

Checked
A.ASHOSH

MOBILE
0414062484

Council
CANTERBURY BANKSTOWN

Job No.
26LUC

Lot/DP
401/261279

PROJECT
PROPOSED DUAL OCCUPANCY

Rev.No
02

Publish Date
18/08/2026

DRAWING TITLE
BASEMENT FOOTING & SLAB LAYOUT


26 LUCINDA AVENUE, BASS HILL, NSW

1:100 A3

DRAWING NO.
ST03

The contractor and / or subcontractors shall be responsible for all levels and dimensions prior to commencing on site or off site constructions and/or fabrications. These drawings must not be scaled. These drawings are dimensioned in (mms).These drawings must be read in conjunction with all other drawings and/or instructions as may be issued during the course of the project.These drawings are copyright and must not be retained, copied, developed or amended without a written consent from RK INFRA. All works resulting of these drawings are to be in accordance with 1- The Building Code of Australia. 2- All codes and regulations of LOCAL AUTHORITY REQUIREMENTS. 3- All related Trades Australian Standards. These drawings are site specific and can only be used for the address as listed in these drawings. These drawings are site specific and can only be used for the address listed in these drawings. 1. All works to be in accordance with the Building Code of Australia. Australian Standards, statutory regulations and local authority requirements. 2. Consistency between similar materials to be maintained. RK INFRA to be notified discrepancies, dimensional inconsistencies or the need for clarification prior to manufacture. 3. RK INFRA to approve all detailed drawings/setting out prior to construction.5. Contractors to confirm stability and feasibility of all units/components manufacture. 6. All drawing measurements to be verified on site - do not scale from documents. 7.Refer to this document in conjunction with Specification or any other plans such as structural, hydraulic and electrical (if applicable) for further information.


WHERE FOOTINGS ARE WIDER THAN THE SPECIFIED WIDTH, AN EXTRA BOTTOM BAR OR EQUIVALENT OF THE SAME BAR SIZE IS REQUIRED FOR EACH 100mm ADDITIONAL WIDTH.

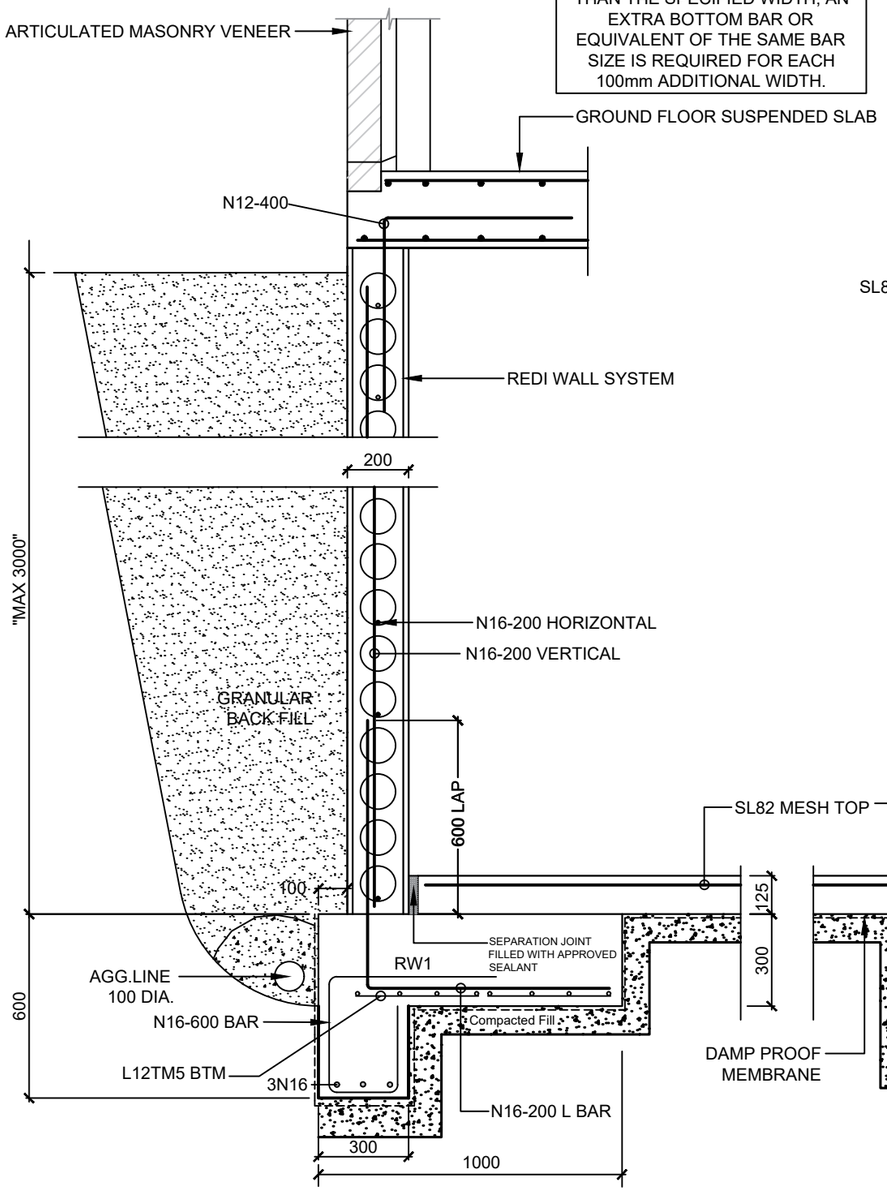

RETAINING WALL (RW1) & RB1 DETAILS


SCALE 1:20


COMPACTED FILL TO BE 250mm MINIMUM UNDER THE FOOTINGS

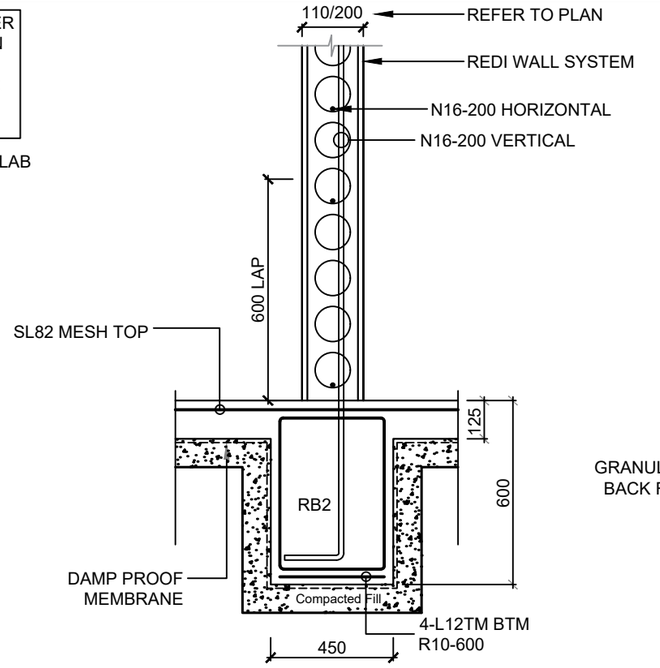

INTERNAL "RB2" DETAIL

NTS

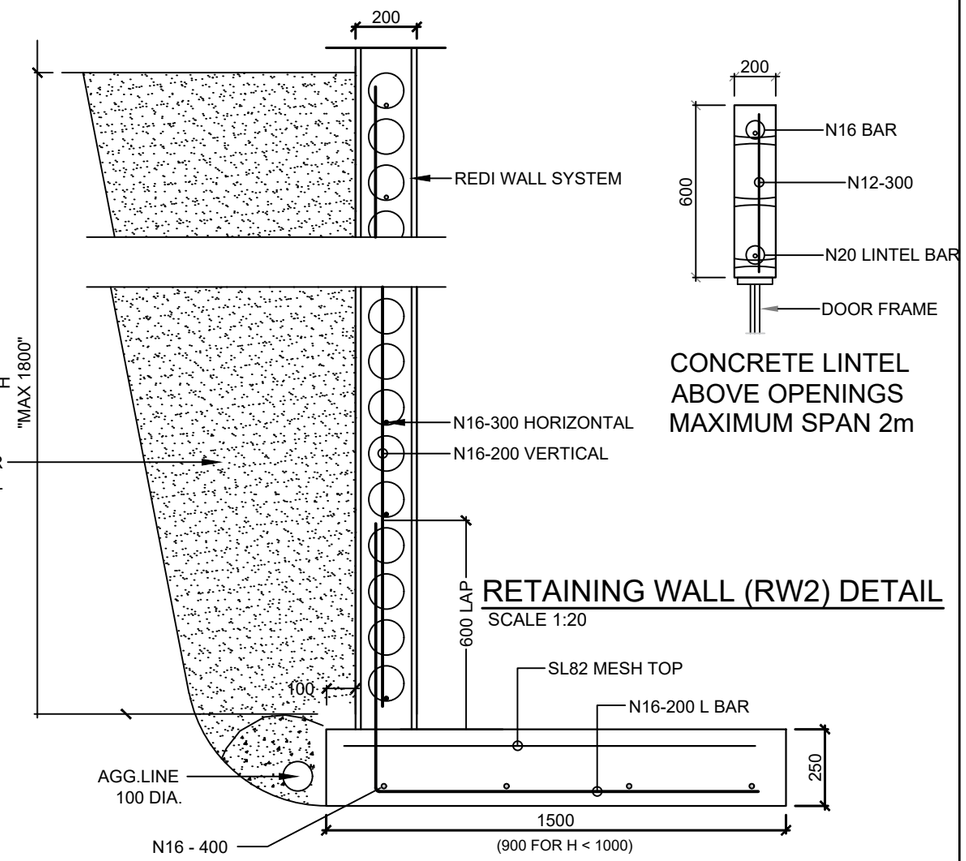


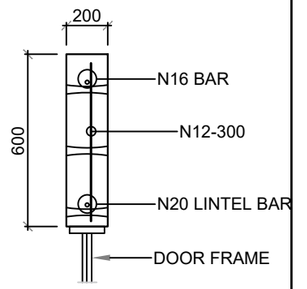

CONCRETE LINTEL ABOVE OPENINGS MAXIMUM SPAN 2m


RETAINING WALL (RW2) DETAIL

SCALE 1:20

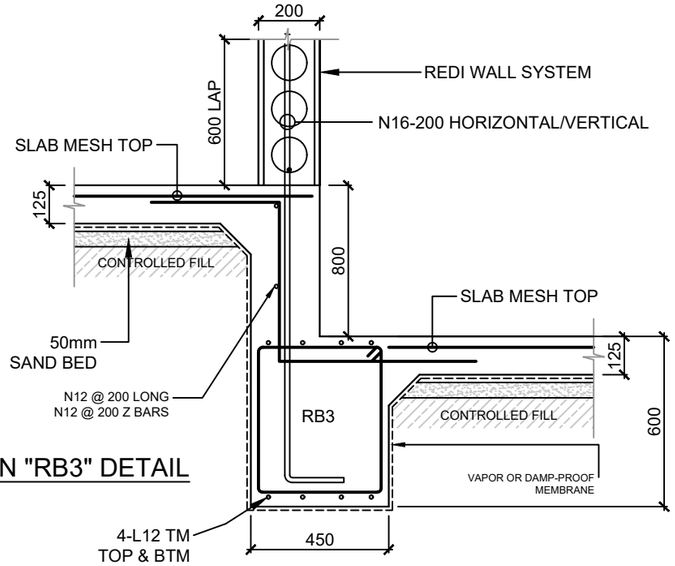

STEP DOWN "RB3" DETAIL

NTS

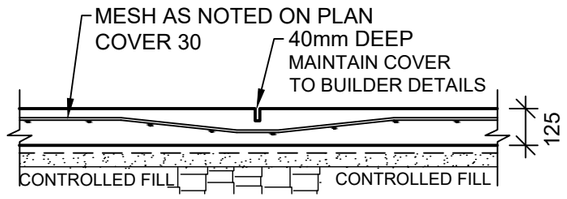

TYPICAL SLAB ON GROUND SECTION

SCALE 1:20


RK INFRA
DESIGN | CONSULTING | DEVELOPMENT

Designed/Drawn M.HOSNI	Checked A.ASHOSH	Council CANTERBURY BANKSTOWN		PROJECT PROPOSED DUAL OCCUPANCY		DRAWING TITLE BASEMENT FOOTING & SLAB DETAILS	1:20 A3
Approved K.NAJJAR	MOBILE 0414062484	Job No. 26LUC	Lot/DP 401/261279	Rev.No 02	Publish Date 18/08/2026	26 LUCINDA AVENUE, BASS HILL, NSW	DRAWING NO. ST04

The contractor and / or subcontractors shall be responsible for all levels and dimensions prior to commencing on site or off site constructions and/or fabrications. These drawings must not be scaled. These drawings are dimensioned in (mms).These drawings must be read in conjunction with all other drawings and/or instructions as may be issued during the course of the project.These drawings are copyright and must not be retained, copied, developed or amended without a written consent from RK INFRA. All works resulting of these drawings are to be in accordance with 1- The Building Code of Australia. 2- All codes and regulations of LOCAL AUTHORITY REQUIREMENTS. 3- All related Trades Australian Standards. These drawings are site specific and can only be used for the address as listed in these drawings. These drawings are site specific and can only be used for the address listed in these drawings. 1. All works to be in accordance with the Building Code of Australia, Australian Standards, statutory regulations and local authority requirements. 2. Consistency between similar materials to be maintained. RK INFRA to be notified discrepancies, dimensional inconsistencies or the need for clarification prior to manufacture. 3. RK INFRA to approve all detailed drawings/setting out prior to construction.5. Contractors to confirm stability and feasibility of all units/components manufacture. 6. All drawing measurements to be verified on site - do not scale from documents. 7.Refer to this document in conjunction with Specification or any other plans such as structural, hydraulic and electrical (if applicable) for further information.


GROUND FLOOR SUSPENDED SLAB LAYOUT

SCALE 1:100

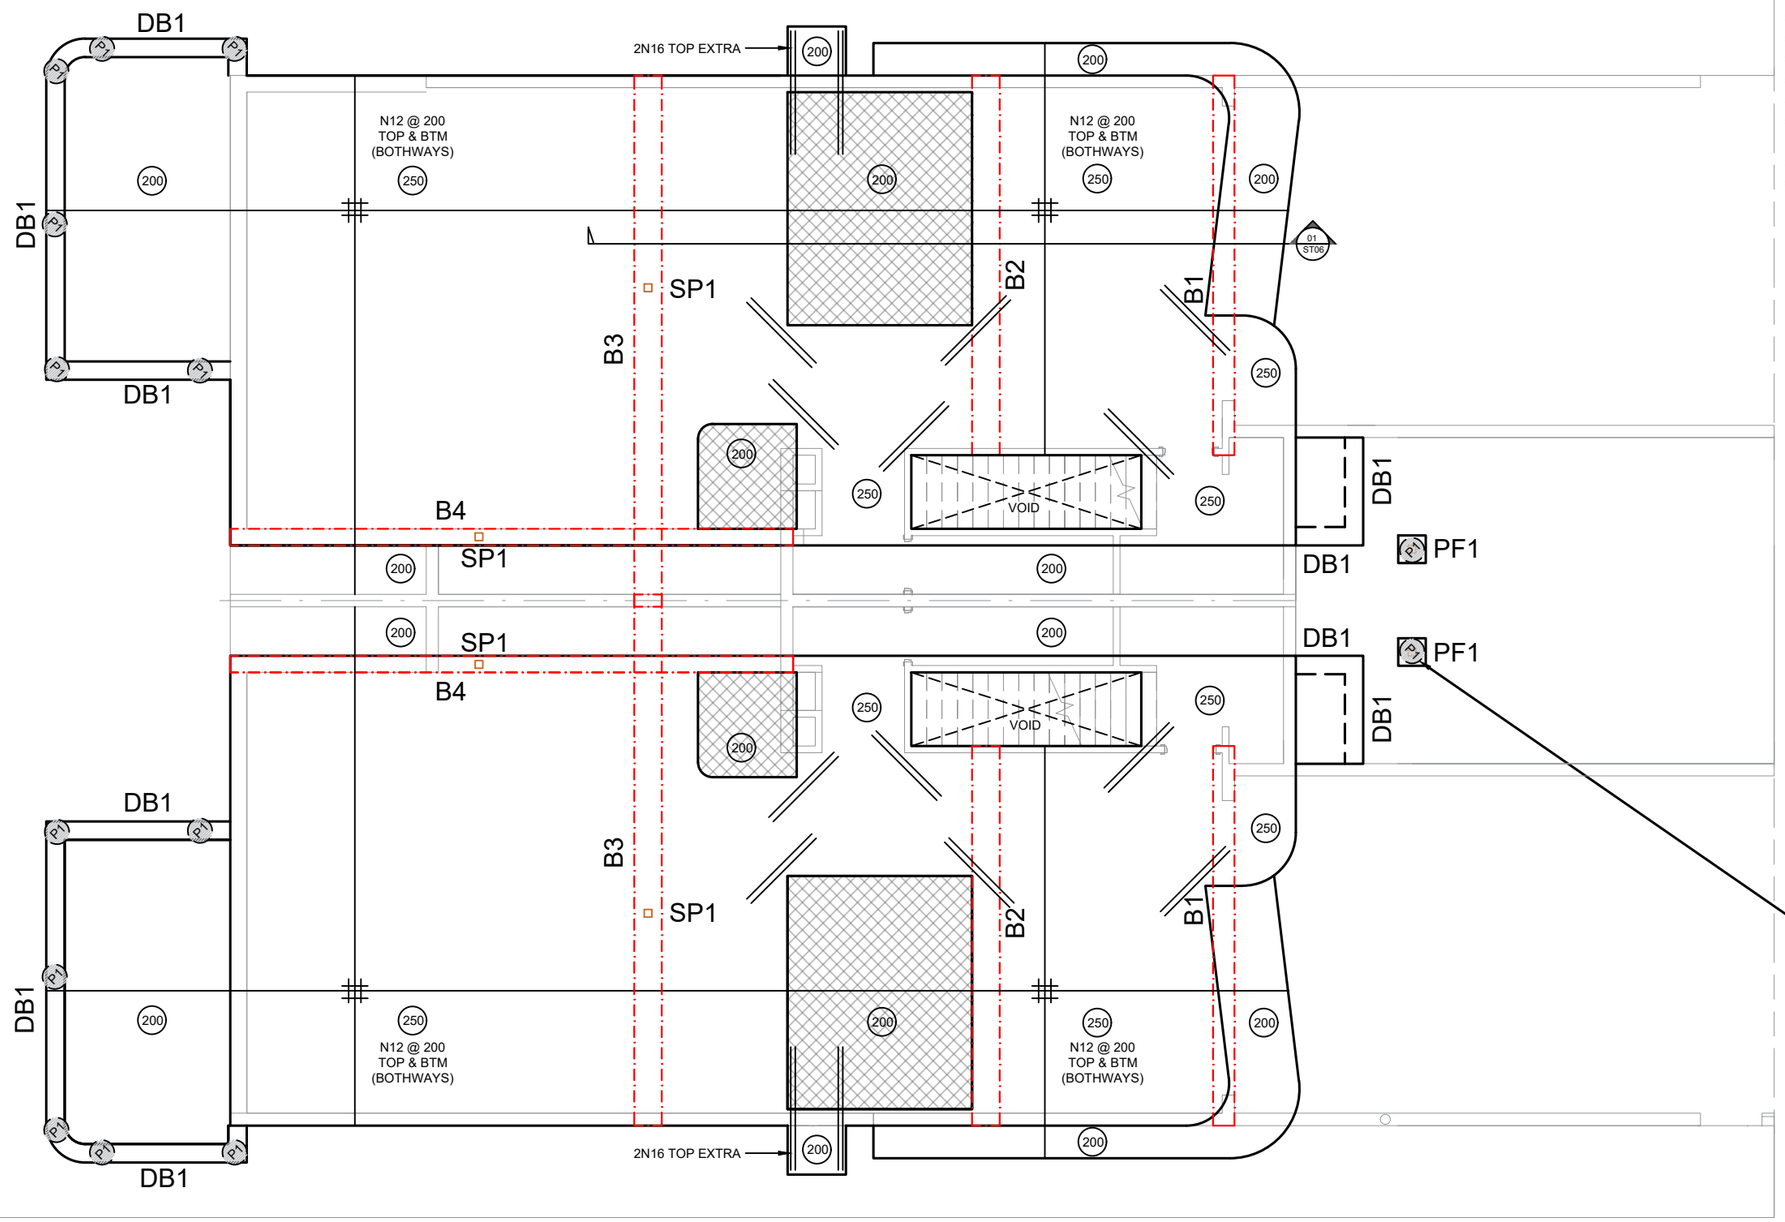

200 250 DENOTES SLAB THICKNESS

- SLAB LEVEL TO BE TAKEN FROM ARCHITECTURAL PLANS.
- MINIMUM SLAB (INTERNAL) COVER TO BE 20mm.
- MINIMUM SLAB (EXTERNAL) COVER TO BE 40mm.
- CONCRETE STRENGTH (fc) = 32MPa.
- SECTIONS TO BE READ CAREFULLY.
- WHERE WALLS ARE SUPPORTED ON SLAB PROVIDE EXTRA N16 BOT
- EXTRA N12 TOP TO BE PROVIDED AT SUPPORT AND BEAMS
- ENSURE BAR CONTINUITY - PROVIDE MIN LAP LENGTH 50x BAR DIAMETER UNO.

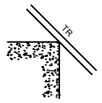

AT RE-ENTRANT CORNERS: PROVIDE 2N12 TRIMMER BARS TOP EXTENDING 600 PAST CORNERS. (2000mm MIN. LENGTH).



AT OPENINGS IN SLAB: UNO PROVIDE 2N12 TOP & BTM BARS EXTENDING 600 PAST CORNERS.

WET AREA

LEGEND	
B1	CONCRETE BEAM. REFER TO DETAILS
B2	CONCRETE BEAM. REFER TO DETAILS
B3	CONCRETE BEAM. REFER TO DETAILS
B4	CONCRETE BEAM. REFER TO DETAILS
DB1	CONCRETE BEAM. REFER TO DETAILS
SP1	150x150x6 SHS STEEL POST (BELOW)
P1	400mm DIA. CONCRETE PILE
PF1	400x400x400 PAD FOOTING. REFER TO DETAILS
	BASEMENT WALLS BELOW

400mm MASS CONCRETE PILE.
TO SAME DEPTH AS BASEMENT FOOTINGS
OR TO ROCK/SHALE LAYER
OR TO GEOTECHNICAL
ENGINEER APPROVED SURFACE.
MAX. 2500 C/C SPACING.

RK INFRA
DESIGN | CONSULTING | DEVELOPMENT

Designed/Drawn
M.HOSNI

Checked
A.ASHOSH

Approved
K.NAJJAR

MOBILE
0414062484

Council
CANTERBURY BANKSTOWN

Job No.
26LUC

Lot/DP
401/261279

PROJECT
PROPOSED DUAL OCCUPANCY

Rev.No
02

Publish Date
18/08/2026


DRAWING TITLE
GROUND FLOOR FOOTING & SLAB LAYOUT

26 LUCINDA AVENUE, BASS HILL, NSW

1:100 A3

DRAWING NO.
ST05

The contractor and / or subcontractors shall be responsible for all levels and dimensions prior to commencing on site or off site constructions and/or fabrications. These drawings must not be scaled. These drawings are dimensioned in (mms).These drawings must be read in conjunction with all other drawings and/or instructions as may be issued during the course of the project.These drawings are copyright and must not be retained, copied, developed or amended without a written consent from RK INFRA. All works resulting of these drawings are to be in accordance with 1- The Building Code of Australia. 2- All codes and regulations of LOCAL AUTHORITY REQUIREMENTS. 3- All related Trades Australian Standards. These drawings are site specific and can only be used for the address as listed in these drawings. These drawings are site specific and can only be used for the address listed in these drawings. 1. All works to be in accordance with the Building Code of Australia, Australian Standards, statutory regulations and local authority requirements. 2. Consistency between similar materials to be maintained. RK INFRA to be notified discrepancies, dimensional inconsistencies or the need for clarification prior to manufacture. 3. RK INFRA to approve all detailed drawings/setting out prior to construction.5. Contractors to confirm stability and feasibility of all units/components manufacture. 6. All drawing measurements to be verified on site - do not scale from documents. 7.Refer to this document in conjunction with Specification or any other plans such as structural, hydraulic and electrical (if applicable) for further information.

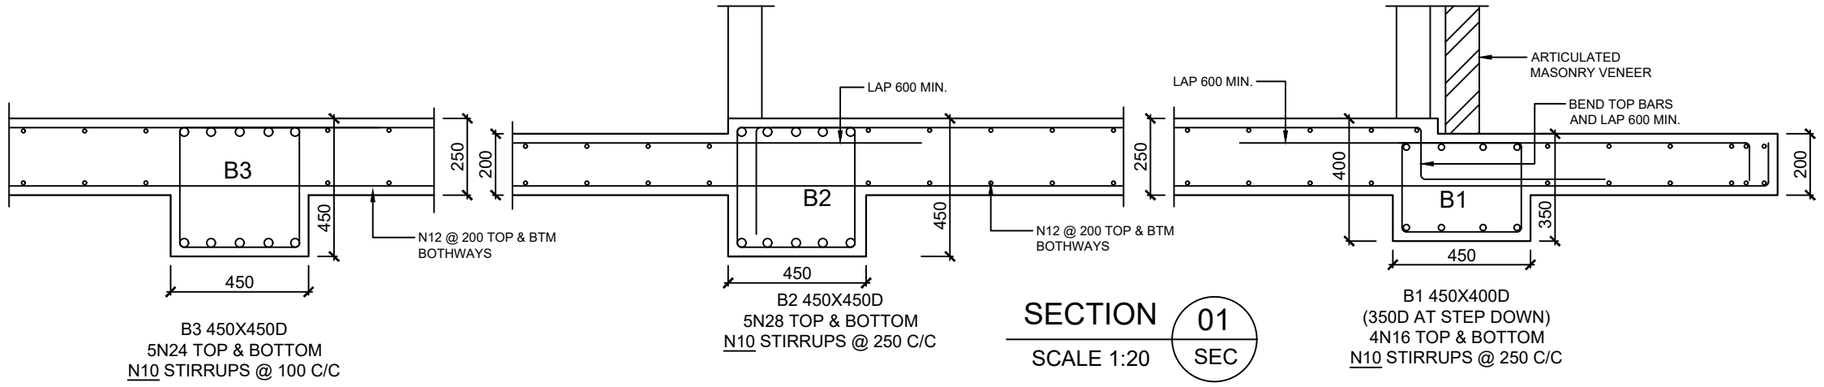


B3 450X450D
5N24 TOP & BOTTOM
N10 STIRRUPS @ 100 C/C

B2 450X450D
5N28 TOP & BOTTOM
N10 STIRRUPS @ 250 C/C


SECTION 01
SCALE 1:20 SEC

B1 450X400D
(350D AT STEP DOWN)
4N16 TOP & BOTTOM
N10 STIRRUPS @ 250 C/C

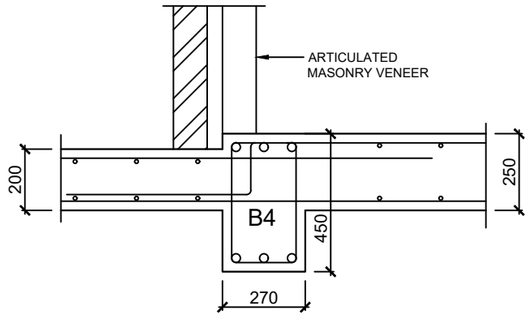



B4 270X450D
3N20 TOP & BOTTOM
N10 STIRRUPS @ 300 C/C

DEEP BEAM REBAR DETAILS		
DROP EDGE BEAM DEPTH	HORIZONTAL REBAR	VERTICAL REBAR
170 - 400mm	1N12	N12-600
410 - 900mm	N12 - 400	N12 - 400
910 - 1500mm	N12 - 300	N12 - 300
1510 - 1800mm	N12 - 200	N12 - 200

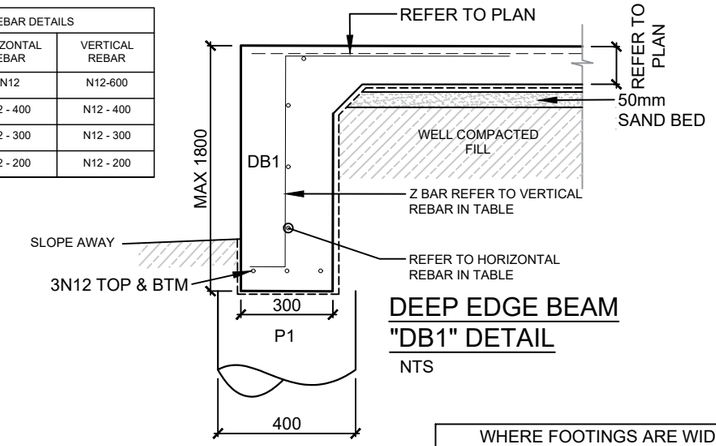

DEEP EDGE BEAM "DB1" DETAIL
NTS

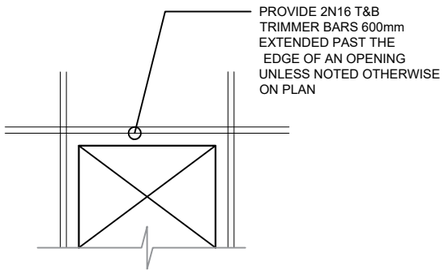


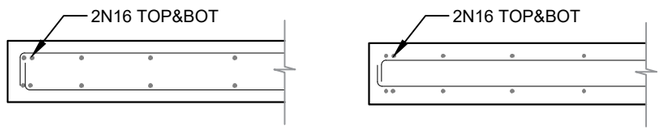


UNO: TRIMMER DETAILS & SLAB ENDS AT AN OPENING
SCALE NTS

WHERE FOOTINGS ARE WIDER THAN THE SPECIFIED WIDTH, AN EXTRA BOTTOM BAR OR EQUIVALENT OF THE SAME BAR SIZE IS REQUIRED FOR EACH 100mm ADDITIONAL WIDTH.


PROVIDE MASONRY ARTICULATION JOINTS AT MAX. 6m INTERVALS IN ACCORDANCE WITH AS3700

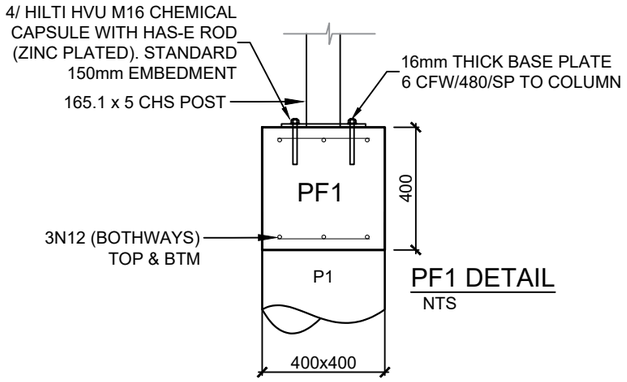

PF1 DETAIL
NTS

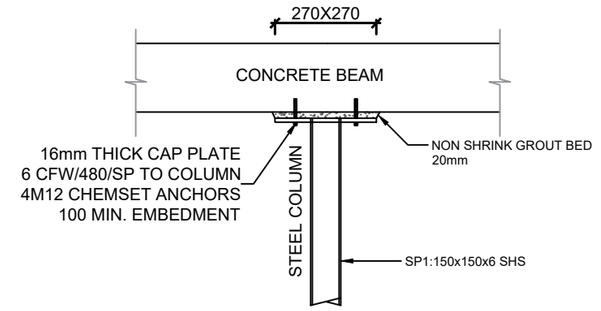

SP1 TO CONCRETE BEAM
NTS

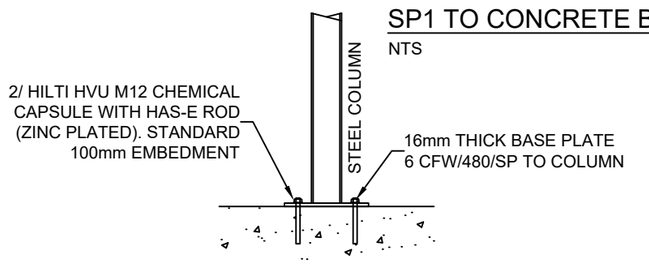


RK INFRA
DESIGN | CONSULTING | DEVELOPMENT

Designed/Drawn M.HOSNI	Checked A.ASHOSH	Council CANTERBURY BANKSTOWN	PROJECT PROPOSED DUAL OCCUPANCY	DRAWING TITLE GROUND FLOOR FOOTING & SLAB DETAILS	26 LUCINDA AVENUE, BASS HILL, NSW	AS SHOWN A3
Approved K.NAJJAR	MOBILE 0414062484	Job No. 26LUC / Lot/DP 401/261279	Rev.No 02 / Publish Date 18/08/2026			DRAWING NO. ST06

The contractor and / or subcontractors shall be responsible for all levels and dimensions prior to commencing on site or off site constructions and/or fabrications. These drawings must not be scaled. These drawings are dimensioned in (mms).These drawings must be read in conjunction with all other drawings and/or instructions as may be issued during the course of the project.These drawings are copyright and must not be retained, copied, developed or amended without a written consent from RK INFRA. All works resulting of these drawings are to be in accordance with 1- The Building Code of Australia. 2- All codes and regulations of LOCAL AUTHORITY REQUIREMENTS. 3- All related Trades Australian Standards. These drawings are site specific and can only be used for the address as listed in these drawings. These drawings are site specific and can only be used for the address listed in these drawings. 1. All works to be in accordance with the Building Code of Australia, Australian Standards, statutory regulations and local authority requirements. 2. Consistency between similar materials to be maintained. RK INFRA to be notified discrepancies, dimensional inconsistencies or the need for clarification prior to manufacture. 3. RK INFRA to approve all detailed drawings/setting out prior to construction.5. Contractors to confirm stability and feasibility of all units/components manufacture. 6. All drawing measurements to be verified on site - do not scale from documents. 7.Refer to this document in conjunction with Specification or any other plans such as structural, hydraulic and electrical (if applicable) for further information.

FIRST FLOOR LAYOUT

SCALE 1:100

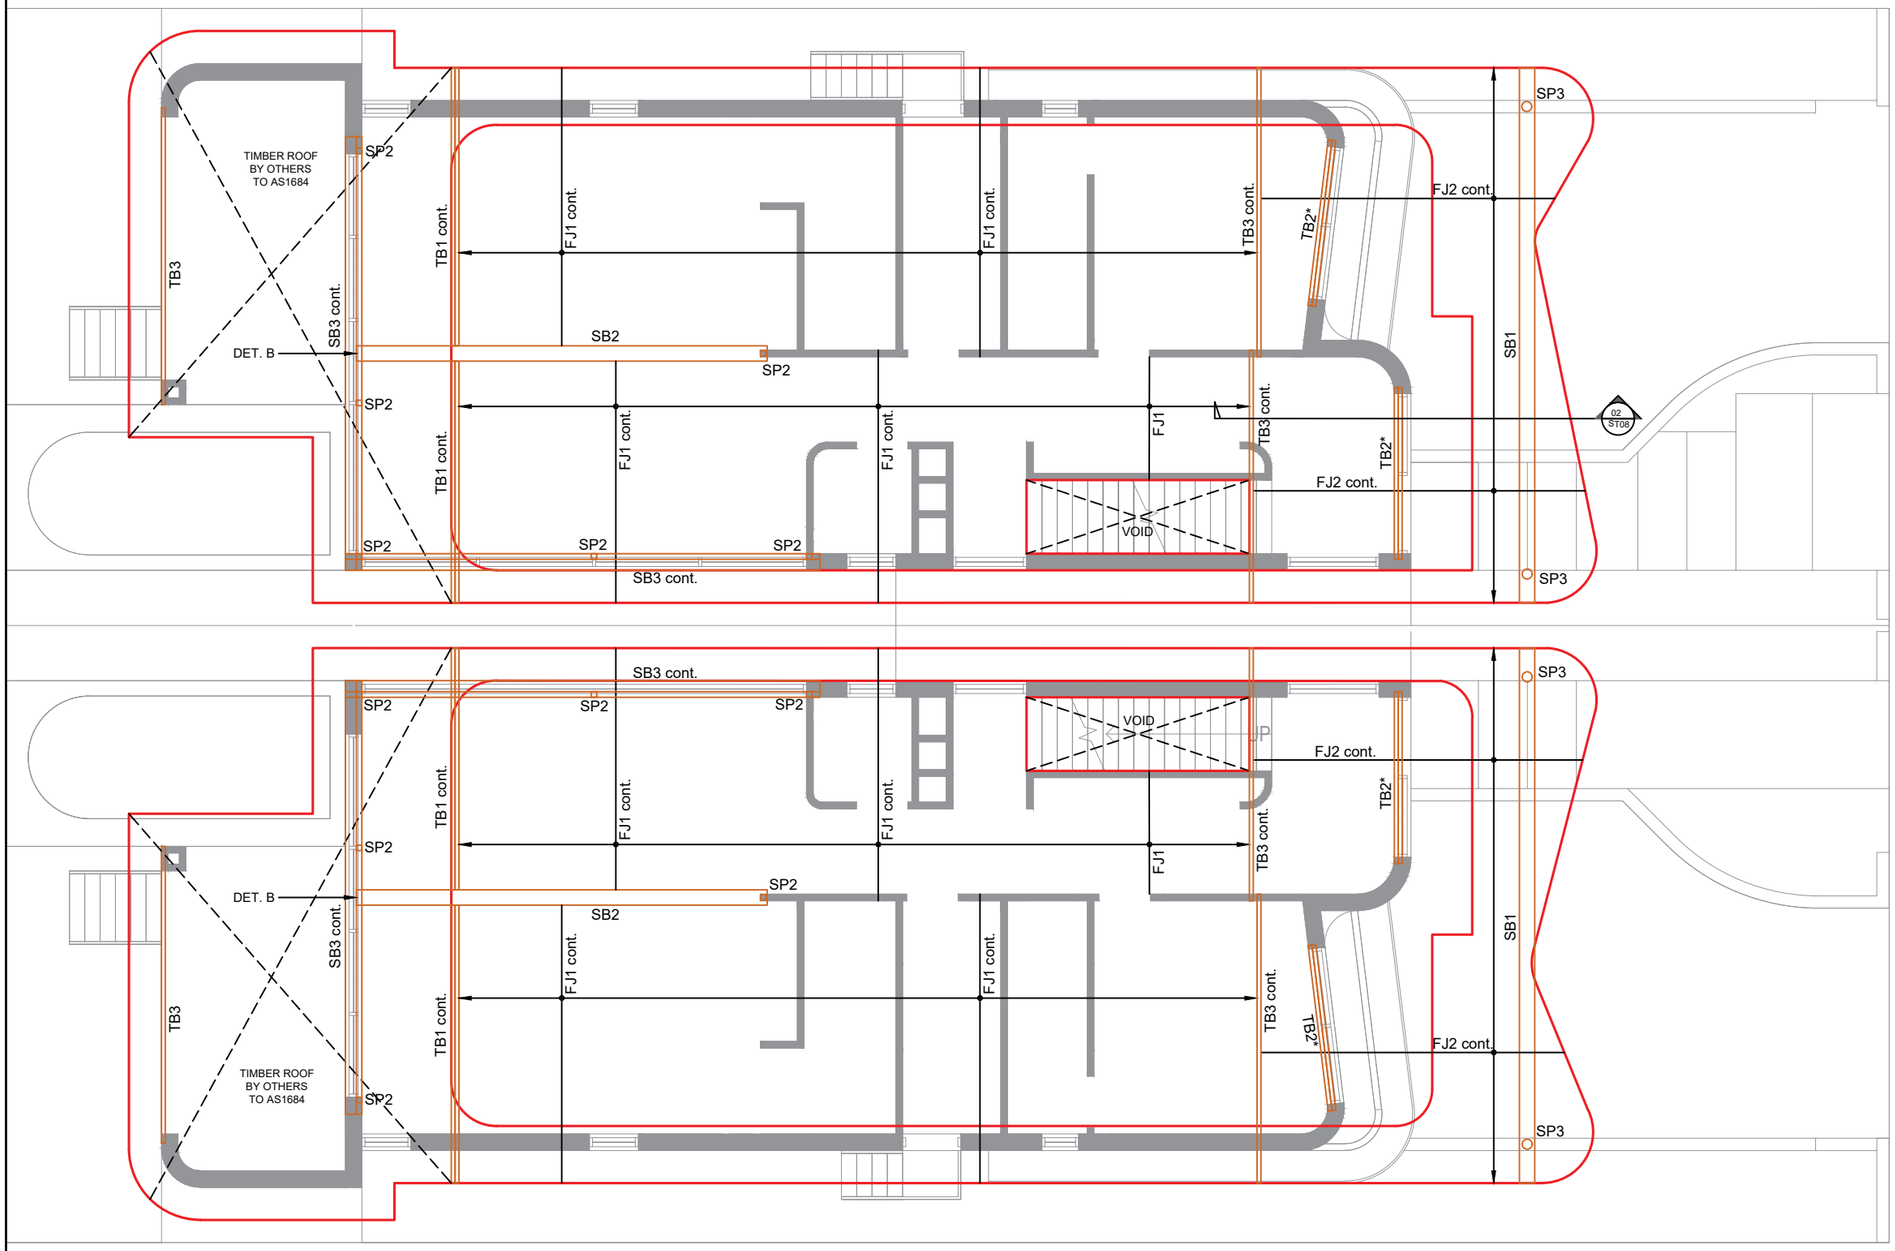

- FINISHED LEVELS TO BE TAKEN FROM ARCHITECTURAL PLANS.
- ALL MEMBERS ARE TO BE hySPAN (LVL) OR EQUIVALENT.
- hySPAN LVL JOISTS, ITI SpecJoist OR EQUIVALENT TO BE USED.
- JOISTS TO BE INSTALLED ACCORDING TO MANUFACTURER SPECIFICATIONS. DO NOT NOTCH I-JOISTS.
- DESIGNED FOR 75mm HEBEL POWERFLOOR.
- STEEL MEMBERS TO BE GRADE 300 MPa UNO.
- NO BRICK WALLS TO BE USED AT THE FIRST FLOOR LEVEL.
- NO BRICK WALLS TO BE FOUNDED ON TIMBER MEMBERS.
- USE DOUBLE JOISTS UNDERNEATH PARALLEL FIRST FLOOR WALLS.
- FAKE PLANTERS TO BE USED ON BALCONY.
- AN ASTERISK (*) NEXT TO MEMBER LABEL DENOTES MEMBER IS BELOW JOISTS/BEAMS

LEGEND			
SB1	250 UC 89.5	SP2	89x89x6 SHS
SB2	250 UC 72.9	SP3	165.1x5 CHS
SB3	250 PFC 90 + 10x230 STEEL PLATE (LINTEL)		
TB1	2x300x45 LVL		
TB2	2x200x63 LVL	*BENEATH JOISTS	
TB3	300x45 LVL		
FJ1	300x45 @ 450 ITI SpecJoists		
FJ2	240x45 @ 450 ITI SpecJoists		
	GROUND FLOOR WALLS		
	FIRST FLOOR LIMITS		

TIMBER FRAMING NOTES

1. ALL TIMBER FRAMING SHALL BE CONSTRUCTED IN ACCORDANCE WITH AS1684 AND THE TIMBER FRAMING MANUAL (UNO).
2. FOR ALL GROUND FLOOR LOAD-BEARING WALLS, PROVIDE 90X45 MGP10 PINE STUDS AT 450mm MAX. C/C (MAX. HEIGHT 3000mm).
3. FOR ALL SINGLE LEVEL OR UPPER LEVEL LOAD-BEARING WALLS, PROVIDE 90X45 MGP10 PINE STUDS, AT 450mm MAX. C/C (MAX. HEIGHT 3000mm). ALTERNATIVELY PROVIDE 90X45 F17 KDHW STUDS, OR EQUIVALENT, AT 450mm MAX. C/C (MAX. HEIGHT 4200mm). PROVIDE DOUBLE 90X45 F17 KDHW STUDS TO EACH SIDE OF OPENINGS.
4. PROVIDE 90X45 MGP10 PINE TOP PLATES FIXED TO EVERY THIRD STUD USING APPROVED PLATE TIES. REMAINING STUDS TO BE SKEW NAILED TO THE PLATE.
5. PROVIDE 90X45 MGP10 PINE BOTTOM PLATES FIXED TO EVERY THIRD STUD USING APPROVED PLATE TIES. REMAINING STUDS TO BE SKEW NAILED.
6. ALL DOUBLE OR TRIPLE MEMBERS TO BE LAMINATED TOGETHER IN ACCORDANCE WITH AS4440. REFER TO DETAILS.

RK INFRA
DESIGN | CONSULTING | DEVELOPMENT

Designed/Drawn
M.HOSNI

Approved
K.NAJJAR

Checked
A.ASHOSH

MOBILE
0414062484

Council
CANTERBURY BANKSTOWN

Job No.
26LUC

Lot/DP
401/261279

PROJECT
PROPOSED DUAL OCCUPANCY

Rev.No
02

Publish Date
18/08/2026


DRAWING TITLE
FIRST FLOOR TIMBER & STEEL LAYOUT

26 LUCINDA AVENUE, BASS HILL, NSW


1:100 A3

DRAWING NO.
ST07


The contractor and / or subcontractors shall be responsible for all levels and dimensions prior to commencing on site or off site constructions and/or fabrications. These drawings must not be scaled. These drawings are dimensioned in (mms).These drawings must be read in conjunction with all other drawings and/or instructions as may be issued during the course of the project.These drawings are copyright and must not be retained, copied, developed or amended without a written consent from RK INFRA. All works resulting of these drawings are to be in accordance with 1- The Building Code of Australia. 2- All codes and regulations of LOCAL AUTHORITY REQUIREMENTS. 3- All related Trades Australian Standards. These drawings are site specific and can only be used for the address as listed in these drawings. These drawings are site specific and can only be used for the address listed in these drawings. 1. All works to be in accordance with the Building Code of Australia, Australian Standards, statutory regulations and local authority requirements. 2. Consistency between similar materials to be maintained. RK INFRA to be notified discrepancies, dimensional inconsistencies or the need for clarification prior to manufacture. 3. RK INFRA to approve all detailed drawings/setting out prior to construction.5. Contractors to confirm stability and feasibility of all units/components manufacture. 6. All drawing measurements to be verified on site - do not scale from documents. 7.Refer to this document in conjunction with Specification or any other plans such as structural, hydraulic and electrical (if applicable) for further information.

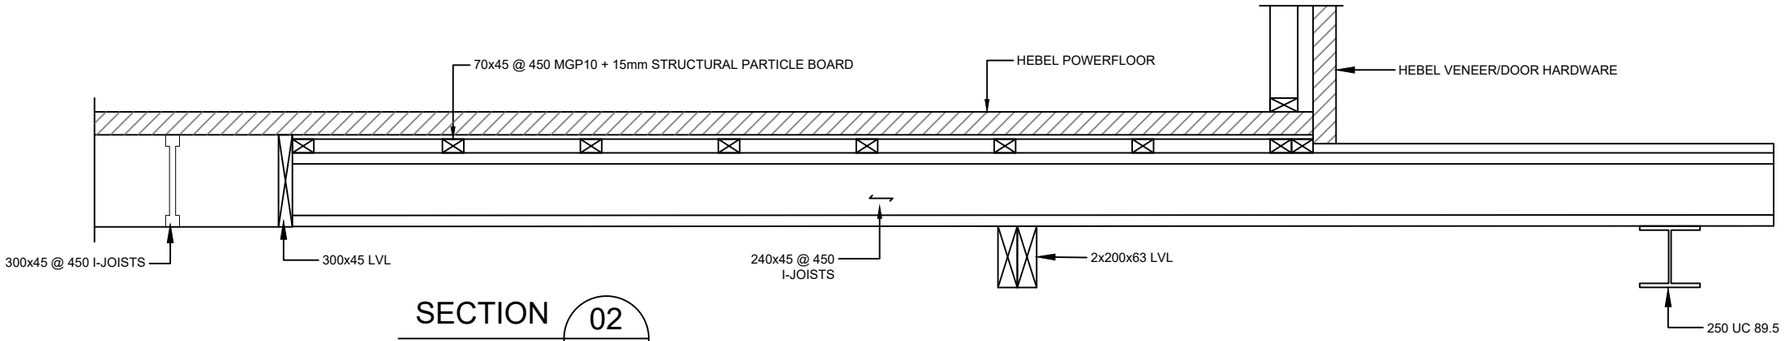


SECTION 02
SCALE 1:20 SEC

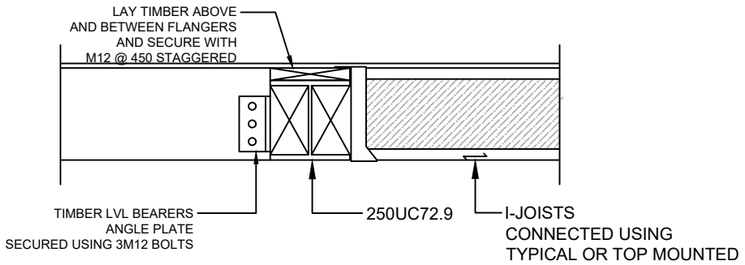


DETAIL A
NTS

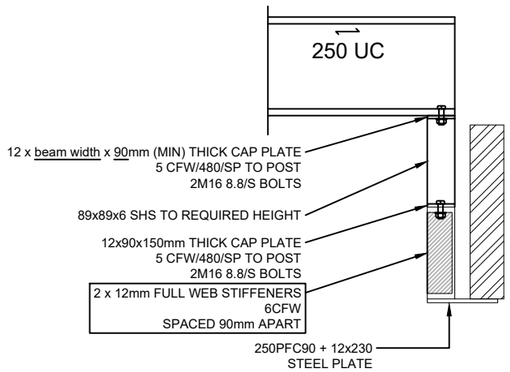


DETAIL B
NTS

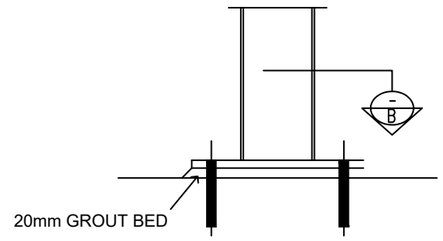


COLUMN BASE PLATE

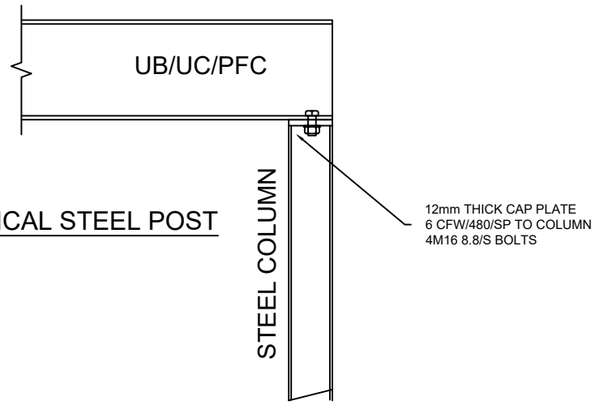

TYPICAL STEEL POST
NTS

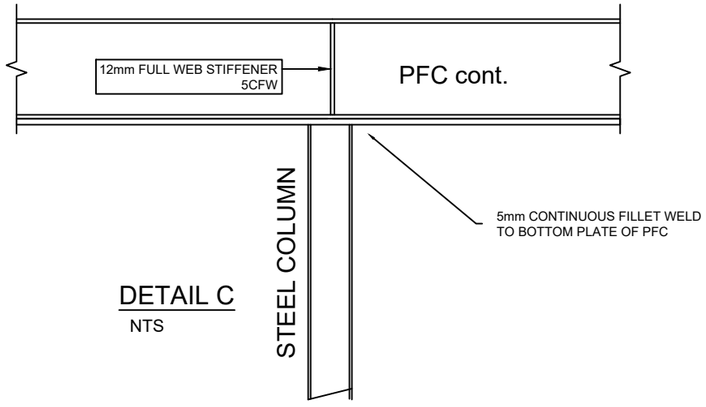

DETAIL C
NTS

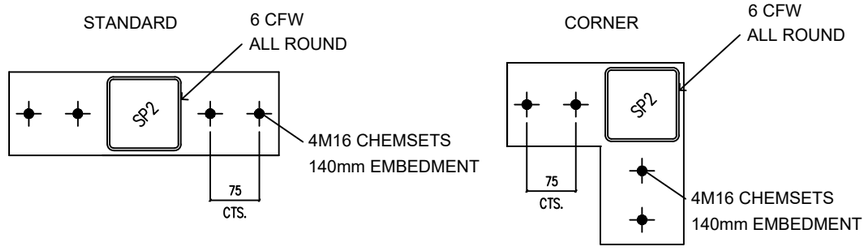


SECTION B-B

RK INFRA
DESIGN | CONSULTING | DEVELOPMENT

Designed/Drawn: M.HOSNI	Checked: A.ASHOSH	Council: CANTERBURY BANKSTOWN	PROJECT: PROPOSED DUAL OCCUPANCY	DRAWING TITLE: FIRST FLOOR DETAILS	26 LUCINDA AVENUE, BASS HILL, NSW	AS SHOWN A3
Approved: K.NAJJAR	MOBILE: 0414062484	Job No.: 26LUC / Lot/DP: 401/261279	Rev.No: 02 / Publish Date: 18/08/2026			DRAWING NO.: ST08


The contractor and / or subcontractors shall be responsible for all levels and dimensions prior to commencing on site or off site constructions and/or fabrications. These drawings must not be scaled. These drawings are dimensioned in (mms).These drawings must be read in conjunction with all other drawings and/or instructions as may be issued during the course of the project.These drawings are copyright and must not be retained, copied, developed or amended without a written consent from RK INFRA. All works resulting of these drawings are to be in accordance with 1- The Building Code of Australia. 2- All codes and regulations of LOCAL AUTHORITY REQUIREMENTS. 3- All related Trades Australian Standards. These drawings are site specific and can only be used for the address as listed in these drawings. These drawings are site specific and can only be used for the address listed in these drawings. 1. All works to be in accordance with the Building Code of Australia, Australian Standards, statutory regulations and local authority requirements. 2. Consistency between similar materials to be maintained. RK INFRA to be notified discrepancies, dimensional inconsistencies or the need for clarification prior to manufacture. 3. RK INFRA to approve all detailed drawings/setting out prior to construction.5. Contractors to confirm stability and feasibility of all units/components manufacture. 6. All drawing measurements to be verified on site - do not scale from documents. 7.Refer to this document in conjunction with Specification or any other plans such as structural, hydraulic and electrical (if applicable) for further information.

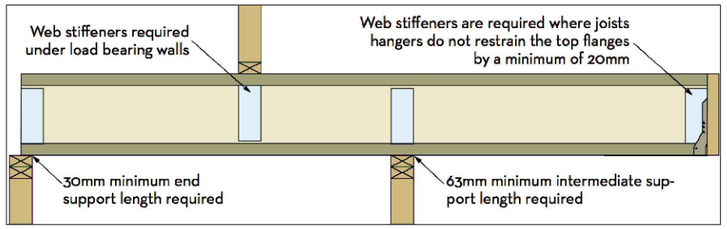

Web Stiffener Requirements for use with Joist Connectors

ADDITIONAL DETAILS FOR i JOISTS


NTS
REFER TO FULL MANUFACTURER SPECIFICATIONS DURING INSTALLATION

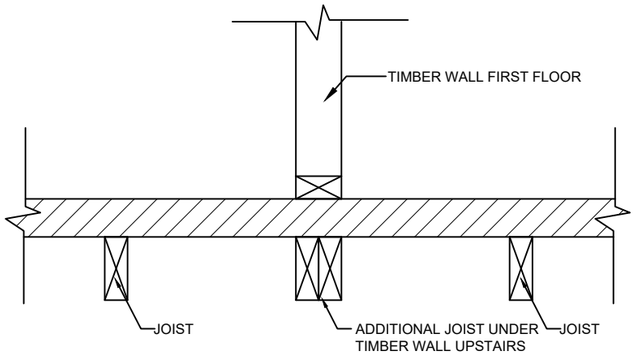


ADDITIONAL SUPPORT DETAIL UNDER TIMBER WALL PARALLEL TO JOISTS

SCALE 1:20


SECTION SIZE "B"	MIN. NAIL DIAMETER	MIN. NAIL LENGTH	BOLT ALTERNATIVE	TRIPPLE BEAM
45	3.30 mm	90 mm	M12 BOLT	M12 BOLT
63	3.30 mm	100 mm	M12 BOLT	M12 BOLT
75			M12 BOLT	M12 BOLT

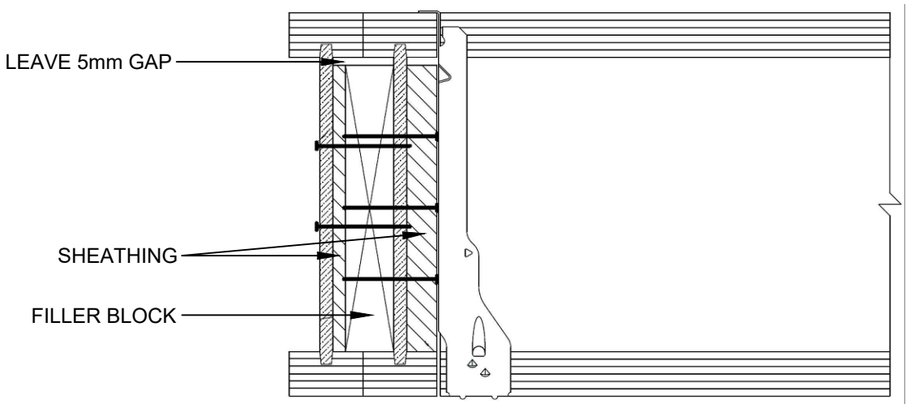


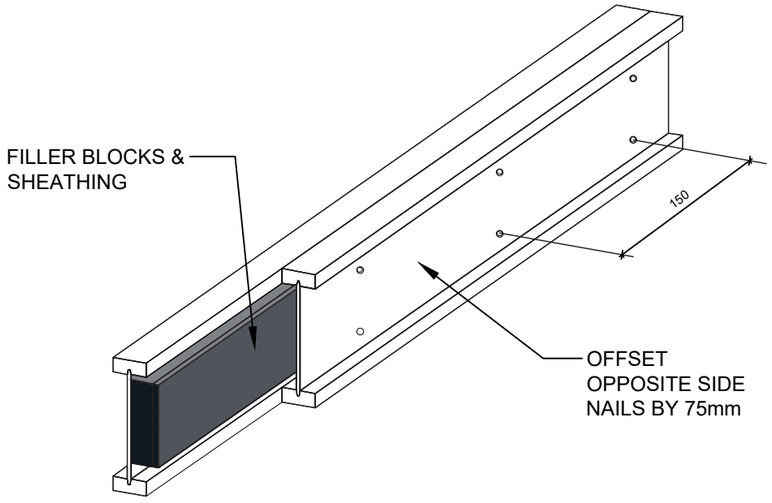

DOUBLE I-JOIST TIE DETAILS

NTS

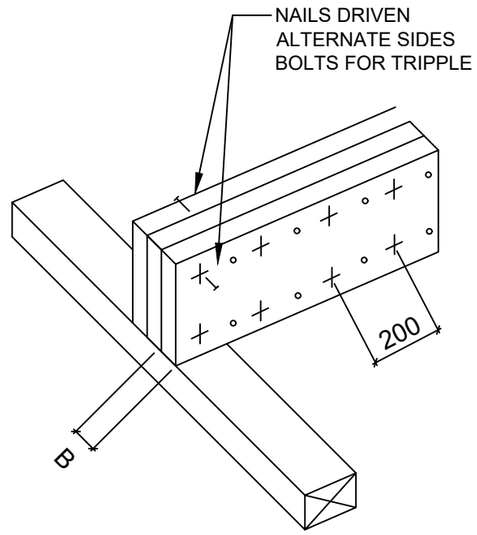

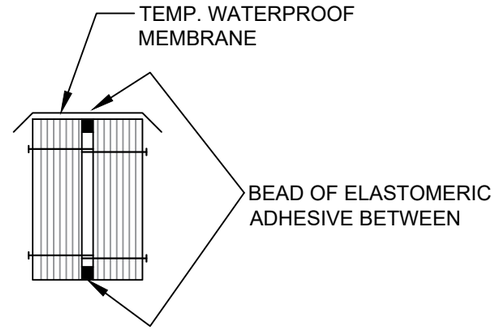


DOUBLE/TRIPPLE BEAM TIE DETAILS

NTS

RK INFRA
DESIGN | CONSULTING | DEVELOPMENT

Designed/Drawn: M.HOSNI	Checked: A.ASHOSH	Council: CANTERBURY BANKSTOWN		PROJECT: PROPOSED DUAL OCCUPANCY		DRAWING TITLE: TIMBER DETAILS	NTS
Approved: K.NAJJAR	MOBILE: 0414062484	Job No.: 26LUC	Lot/DP: 401/261279	Rev.No: 02	Publish Date: 18/08/2026	26 LUCINDA AVENUE, BASS HILL, NSW	DRAWING NO.: ST09

The contractor and / or subcontractors shall be responsible for all levels and dimensions prior to commencing on site or off site constructions and/or fabrications. These drawings must not be scaled. These drawings are dimensioned in (mms).These drawings must be read in conjunction with all other drawings and/or instructions as may be issued during the course of the project.These drawings are copyright and must not be retained, copied, developed or amended without a written consent from RK INFRA. All works resulting of these drawings are to be in accordance with 1- The Building Code of Australia. 2- All codes and regulations of LOCAL AUTHORITY REQUIREMENTS. 3- All related Trades Australian Standards. These drawings are site specific and can only be used for the address as listed in these drawings. These drawings are site specific and can only be used for the address listed in these drawings. 1. All works to be in accordance with the Building Code of Australia, Australian Standards, statutory regulations and local authority requirements. 2. Consistency between similar materials to be maintained. RK INFRA to be notified discrepancies, dimensional inconsistencies or the need for clarification prior to manufacture. 3. RK INFRA to approve all detailed drawings/setting out prior to construction.5. Contractors to confirm stability and feasibility of all units/components manufacture. 6. All drawing measurements to be verified on site - do not scale from documents. 7.Refer to this document in conjunction with Specification or any other plans such as structural, hydraulic and electrical (if applicable) for further information.

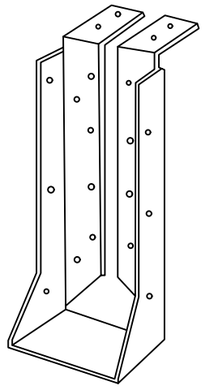


TRIPPLE GRIPS

LINTEL SCHEDULE LVL – SINGLE STOREY

	STUD WALL		CAVITY BRICKWORK (MASONRY OPENING)		
SPAN (mm)	hySPAN LVL	Min. End Bearing	STEEL	T-Bar	Min. End Bearing
900	90x45 hySPAN	50 mm	90x10 PL	180 Cavi-T-Bar	110 mm
1200	120x45 hySPAN	50 mm	90x90x6 EA	180 Cavi-T-Bar	110 mm
1500	140x45 hySPAN	50 mm	90x90x8 EA	180 Cavi-T-Bar	150 mm
1800	170x45 hySPAN	50 mm	90x90x8 EA	180 Cavi-T-Bar	150 mm
2100	190x45 hySPAN	65 mm	90x90x10 EA	180 Cavi-T-Bar	230 mm
2400	240x45 hySPAN	65 mm	150x90x8 L	180 Cavi-T-Bar	230 mm
2700	290x45 hySPAN	75 mm	150x90x10 L	180 Cavi-T-Bar	230 mm
3000	300x63 hySPAN	75 mm	200 PFC + 10 PL	240 Cavi-T-Bar	230 mm
4000	360x63 hySPAN	100 mm	200 PFC + 10 PL	240 Cavi-T-Bar	230 mm


LINTEL SCHEDULE LVL – DOUBLE STOREY

	STUD WALL		CAVITY BRICKWORK (MASONRY OPENING)		
SPAN (mm)	hySPAN LVL	Min. End Bearing	STEEL	T-Bar	Min. End Bearing
900	130x35 hySPAN	50 mm	100x100x8 EA	180 Cavi-T-Bar	110 mm
1200	140x45 hySPAN	50 mm	150x90x8 UA	180 Cavi-T-Bar	110 mm
1500	170x45 hySPAN	50 mm	150x90x10 UA	180 Cavi-T-Bar	150 mm
1800	200x45 hySPAN	65 mm	150x100x10 UA	180 Cavi-T-Bar	150 mm
2100	240x45 hySPAN	65 mm	150 PFC	180 Cavi-T-Bar	230 mm
2400	2/200x45 hySPAN	75 mm	180 PFC	180 Cavi-T-Bar	230 mm
2700	2/240x45 hySPAN	75 mm	200 PFC + 10 PL	240 Cavi-T-Bar	230 mm
3000	2/300x45 hySPAN	90 mm	200 PFC + 12 PL	240 Cavi-T-Bar	230 mm
4000	2/360x63 hySPAN	100 mm	300 PFC + 12 PL	–	230 mm

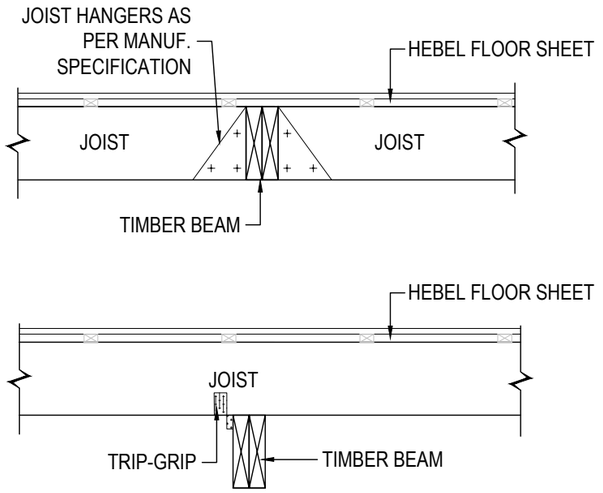


TYPICAL JOIST TO BEAM DETAIL

SCALE 1:20

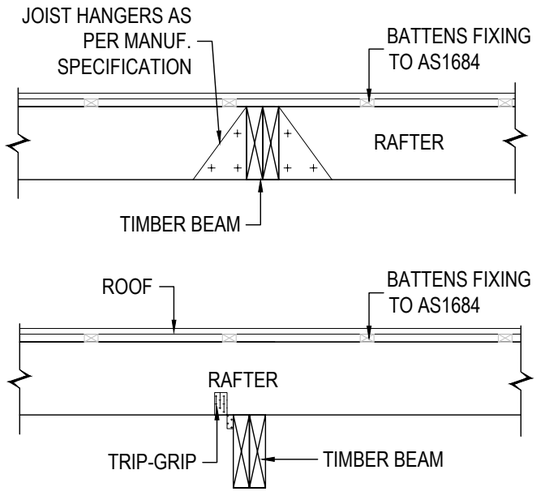


TYPICAL RAFTER TO BEAM DETAIL

SCALE 1:20

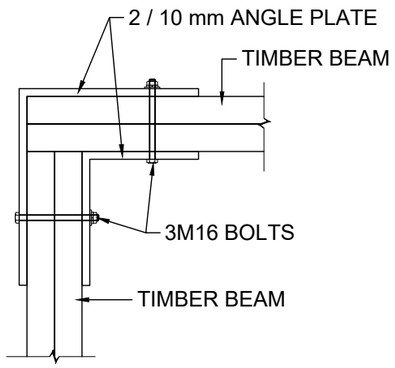

CORNER TIMBER BEAM CONNECTION DETAIL

SCALE 1:20

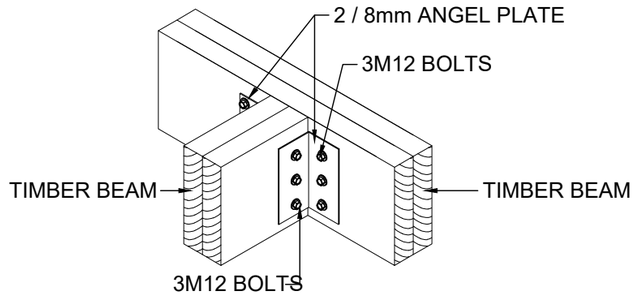


TYPICAL TIMBER BEAM CONNECTION DETAIL

SCALE 1:20


RK INFRA
DESIGN | CONSULTING | DEVELOPMENT

Designed/Drawn M.HOSNI	Checked A.ASHOSH	Council CANTERBURY BANKSTOWN		PROJECT PROPOSED DUAL OCCUPANCY		DRAWING TITLE LINTEL SCHEDULE & TIMBER DETAILS	AS SHOWN A3
Approved K.NAJJAR	MOBILE 0414062484	Job No. 26LUC	Lot/DP 401/261279	Rev.No 02	Publish Date 18/08/2026	26 LUCINDA AVENUE, BASS HILL, NSW	DRAWING NO. ST10


The contractor and / or subcontractors shall be responsible for all levels and dimensions prior to commencing on site or off site constructions and/or fabrications. These drawings must not be scaled. These drawings are dimensioned in (mms).These drawings must be read in conjunction with all other drawings and/or instructions as may be issued during the course of the project.These drawings are copyright and must not be retained, copied, developed or amended without a written consent from RK INFRA. All works resulting of these drawings are to be in accordance with 1- The Building Code of Australia. 2- All codes and regulations of LOCAL AUTHORITY REQUIREMENTS. 3- All related Trades Australian Standards. These drawings are site specific and can only be used for the address as listed in these drawings. These drawings are site specific and can only be used for the address listed in these drawings. 1. All works to be in accordance with the Building Code of Australia, Australian Standards, statutory regulations and local authority requirements. 2. Consistency between similar materials to be maintained. RK INFRA to be notified discrepancies, dimensional inconsistencies or the need for clarification prior to manufacture. 3. RK INFRA to approve all detailed drawings/setting out prior to construction.5. Contractors to confirm stability and feasibility of all units/components manufacture. 6. All drawing measurements to be verified on site - do not scale from documents. 7.Refer to this document in conjunction with Specification or any other plans such as structural, hydraulic and electrical (if applicable) for further information.

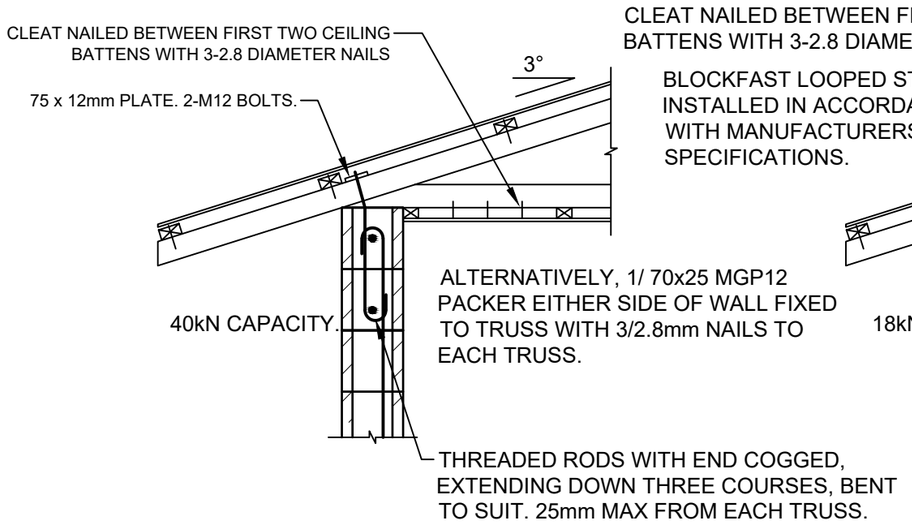


TRUSS TIE DOWN DETAIL
1:20

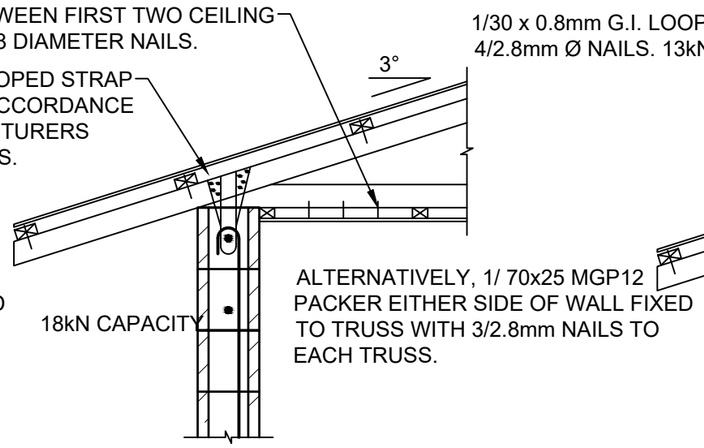


TRUSS TIE DOWN DETAIL
1:20

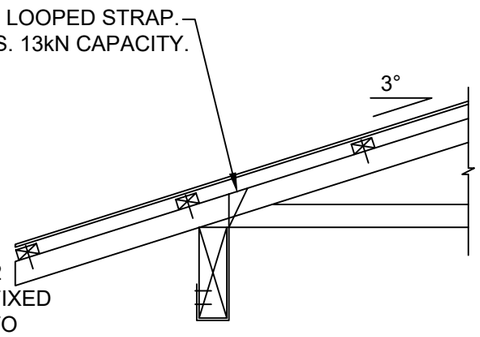


TRUSS TO ROOF BEAM DETAIL
1:20

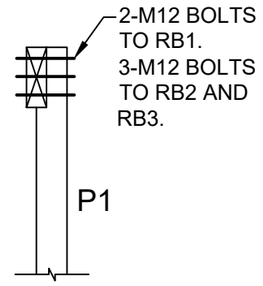


ROOF BEAM TO P1 DETAIL
1:20

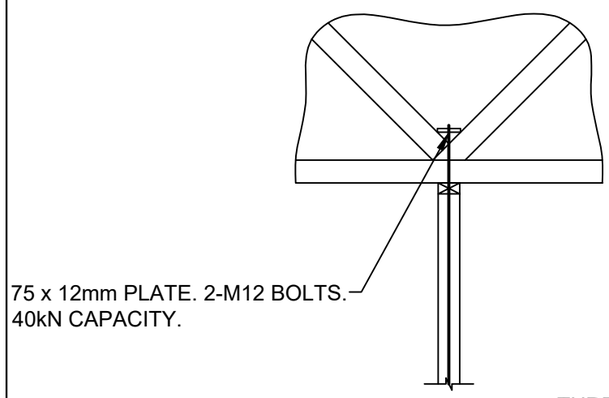

TRUSS TO WALL DETAIL
1:20

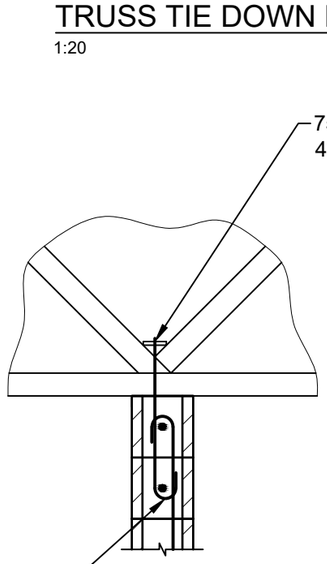

TRUSS TO WALL DETAIL
1:20

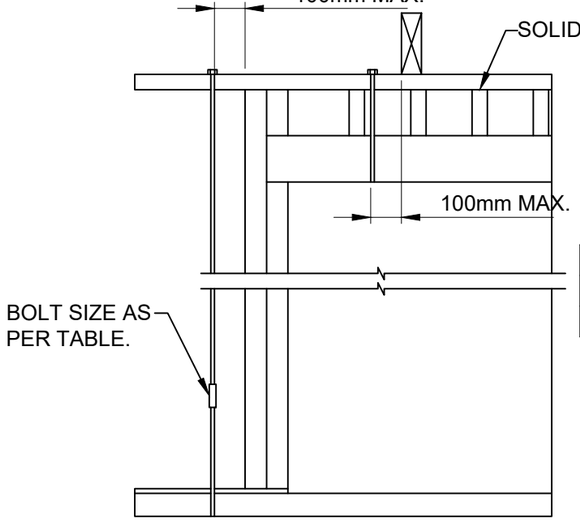

	J2	J3	J4	JD4	JD5	JD6
M12 BOLT	27	27	26	20	16	12
M16 BOLT	50	50	46	35	28	21


NOTE:
THE TOP PLATE SHALL BE FIXED TO THE LINTEL WITHIN 100mm OF EACH RAFTER/TRUSS.

LINTEL TIE DOWN DETAIL
NTS


RK INFRA
DESIGN | CONSULTING | DEVELOPMENT

Designed/Drawn: M.HOSNI	Checked: A.ASHOSH	Council: CANTERBURY BANKSTOWN	PROJECT: PROPOSED DUAL OCCUPANCY	DRAWING TITLE: TIMBER DETAILS	26 LUCINDA AVENUE, BASS HILL, NSW	AS SHOWN A3
Approved: K.NAJJAR	MOBILE: 0414062484	Job No.: 26LUC / Lot/DP: 401/261279	Rev.No: 02 / Publish Date: 18/08/2026			DRAWING NO.: ST11


The contractor and / or subcontractors shall be responsible for all levels and dimensions prior to commencing on site or off site constructions and/or fabrications. These drawings must not be scaled. These drawings are dimensioned in (mms).These drawings must be read in conjunction with all other drawings and/or instructions as may be issued during the course of the project.These drawings are copyright and must not be retained, copied, developed or amended without a written consent from RK INFRA. All works resulting of these drawings are to be in accordance with 1- The Building Code of Australia. 2- All codes and regulations of LOCAL AUTHORITY REQUIREMENTS. 3- All related Trades Australian Standards. These drawings are site specific and can only be used for the address as listed in these drawings. These drawings are site specific and can only be used for the address listed in these drawings. 1. All works to be in accordance with the Building Code of Australia, Australian Standards, statutory regulations and local authority requirements. 2. Consistency between similar materials to be maintained. RK INFRA to be notified discrepancies, dimensional inconsistencies or the need for clarification prior to manufacture. 3. RK INFRA to approve all detailed drawings/setting out prior to construction.5. Contractors to confirm stability and feasibility of all units/components manufacture. 6. All drawing measurements to be verified on site - do not scale from documents. 7.Refer to this document in conjunction with Specification or any other plans such as structural, hydraulic and electrical (if applicable) for further information.

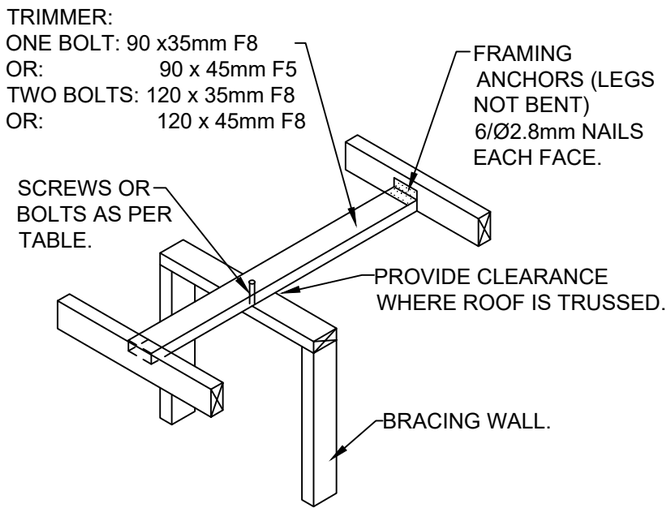

	J2	J3	J4	JD4	JD5	JD6
SCREWS						
1/No.14 TYPE17	4.8	3.5	2.5	3.5	2.5	1.8
2/No.14 TYPE 17	9.7	6.9	4.9	6.9	4.9	3.6
3/No.14 TYPE 17	13	9.3	6.6	9.8	7.4	5.4
BOLTS						
M10	6.4	4.1	2.6	4.3	3.0	2
M12	7.6	4.9	3.1	5.1	3.6	2.5
2/M10	12	8.0	5.1	8.4	5.9	4.0
2/M12	13	9.3	6.1	9.8	7.0	4.9

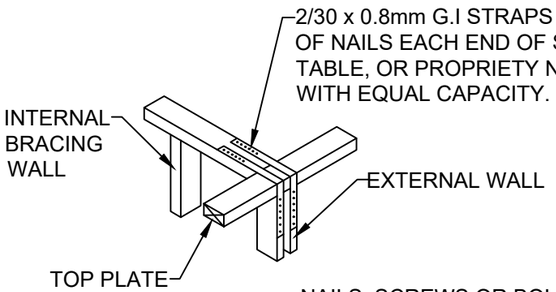


		J2	J3	J4	JD5	JD6	
STRAPS NAILS							
1	4/2.8	4.3	3.1	2.2	3.3	3.0	2.1
	6/2.8	6.5	4.6	3.3	4.9	4.0	3.1
2	4/2.8	8.7	6.2	4.4	6.6	5.4	4.1
	6/2.8	13	9.3	6.6	9.8	8.1	6.1

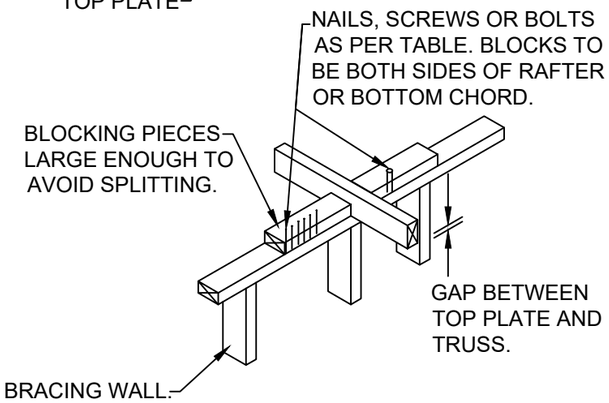


	J2	J3	J4	JD4	JD5	JD6
NAILS						
4/3.05	5.0	3.6	2.5	3.6	3.0	2.2
6/3.05	6.6	4.7	3.4	5.0	4.2	3.1
4/3.33	5.6	4.0	2.8	4.0	3.3	2.5
6/3.33	7.4	5.3	3.7	5.5	4.6	3.5
BOLTS						
M10	6.4	4.1	2.6	4.3	3.0	2.0
M12	7.6	4.9	3.1	5.1	3.6	2.5
2/M10	13	8.0	5.1	8.4	5.9	4.0
SCREWS						
2/No. 14 TYPE 17	9.7	6.9	4.9	6.9	4.9	3.6
3/No. 14 TYPE 17	15	10	7.4	10	7.4	5.4


PLYWOOD SHALL BE NAILED TO FRAME USING 30 x 2.8Ø GALVANISED FLATHEAD NAILS OR EQUIVALENT.
M12 RODS SHALL BE USED AT EACH END OF SHEATHED SECTION TOP PLATE TO BOTTOM PLATE/FLOOR FRAME.

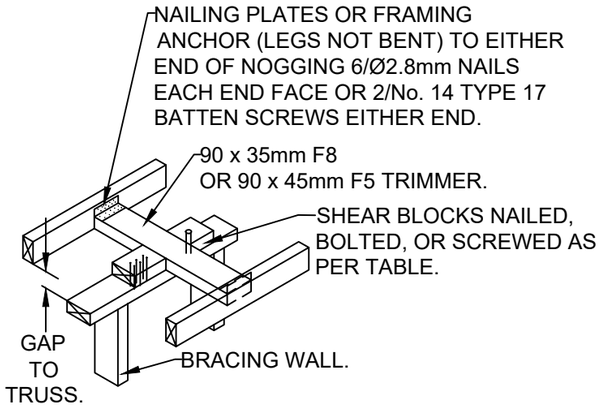

	J2	J3	J4	JD4	JD5	JD6
NAILS						
4/3.05	5.0	3.6	2.5	3.6	3.0	2.2
6/3.05	6.6	4.7	3.4	5.0	4.2	3.1
4/3.33	5.6	4.0	2.8	4.0	3.3	2.5
6/3.33	7.4	5.3	3.7	5.5	4.6	3.5
BOLTS						
M10	6.4	4.1	2.6	4.3	3.0	2.0
M12	7.6	4.9	3.1	5.1	3.6	2.5
2/M10	13	8.0	5.1	8.4	5.9	4.0
SCREWS						
2/No. 14 TYPE 17	9.7	6.9	4.9	6.9	4.9	3.6
3/No. 14 TYPE 17	13	9.2	6.6	9.8	7.4	5.4

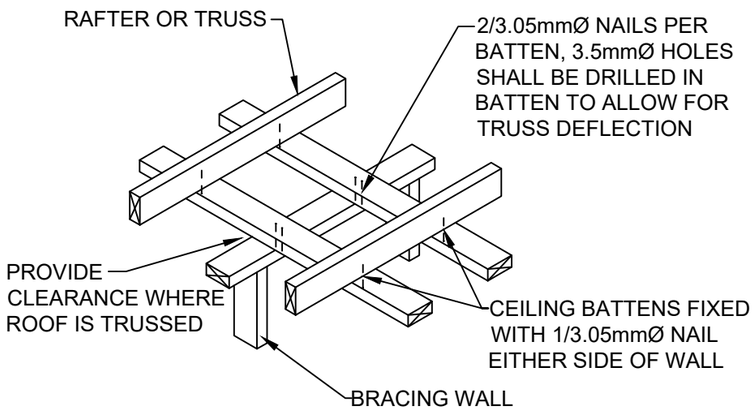

J2	J3	J4	JD4	JD5	JD6
2.5	1.8	1.3	1.8	1.5	1.1

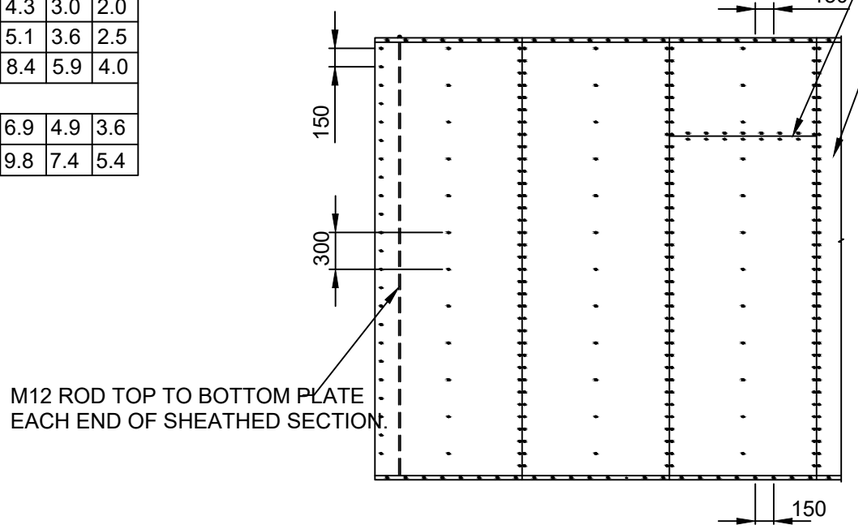

HORIZONTAL BUTT JOINTS PERMITTED, PROVIDED NAIL FIXED TO NOGGING AT 150mm CENTRES.

SHEATHED PANELS SHALL BE CONNECTED TO SLAB WITH M12 CHEMSETS AT 1200mm MAXIMUM CENTRES.

MINIMUM PLYWOOD THICKNESS (mm)		
STRESS GRADE	STUD SPACING (mm)	
	450	600
F11	6	7
F14	4	7

FIXING OF BOTTOM PLATE TO FLOOR FRAME OR SLAB:
M12 RODS AS SHOWN PLUS A 13 kN CAPACITY CONNECTION AT MAXIMUM 1200mm CENTRES.


SINGLE SIDED PLYWOOD BRACING WALL: 6.4kN/m CAPACITY


NTS

RK INFRA
DESIGN | CONSULTING | DEVELOPMENT

Designed/Drawn	Checked	Council	PROJECT		DRAWING TITLE		NTS
M.HOSNI	A.ASHOSH	CANTERBURY BANKSTOWN	PROPOSED DUAL OCCUPANCY		BRACING DETAILS	26 LUCINDA AVENUE, BASS HILL, NSW	DRAWING NO.
Approved	MOBILE	Job No.	Lot/DP	Rev.No	Publish Date		ST12
K.NAJJAR	0414062484	26LUC	401/261279	02	18/08/2026		

The contractor and / or subcontractors shall be responsible for all levels and dimensions prior to commencing on site or off site constructions and/or fabrications. These drawings must not be scaled. These drawings are dimensioned in (mms).These drawings must be read in conjunction with all other drawings and/or instructions as may be issued during the course of the project.These drawings are copyright and must not be retained, copied, developed or amended without a written consent from RK INFRA. All works resulting of these drawings are to be in accordance with 1- The Building Code of Australia. 2- All codes and regulations of LOCAL AUTHORITY REQUIREMENTS. 3- All related Trades Australian Standards. These drawings are site specific and can only be used for the address as listed in these drawings. These drawings are site specific and can only be used for the address listed in these drawings. 1. All works to be in accordance with the Building Code of Australia, Australian Standards, statutory regulations and local authority requirements. 2. Consistency between similar materials to be maintained. RK INFRA to be notified discrepancies, dimensional inconsistencies or the need for clarification prior to manufacture. 3. RK INFRA to approve all detailed drawings/setting out prior to construction.5. Contractors to confirm stability and feasibility of all units/components manufacture. 6. All drawing measurements to be verified on site - do not scale from documents. 7.Refer to this document in conjunction with Specification or any other plans such as structural, hydraulic and electrical (if applicable) for further information.

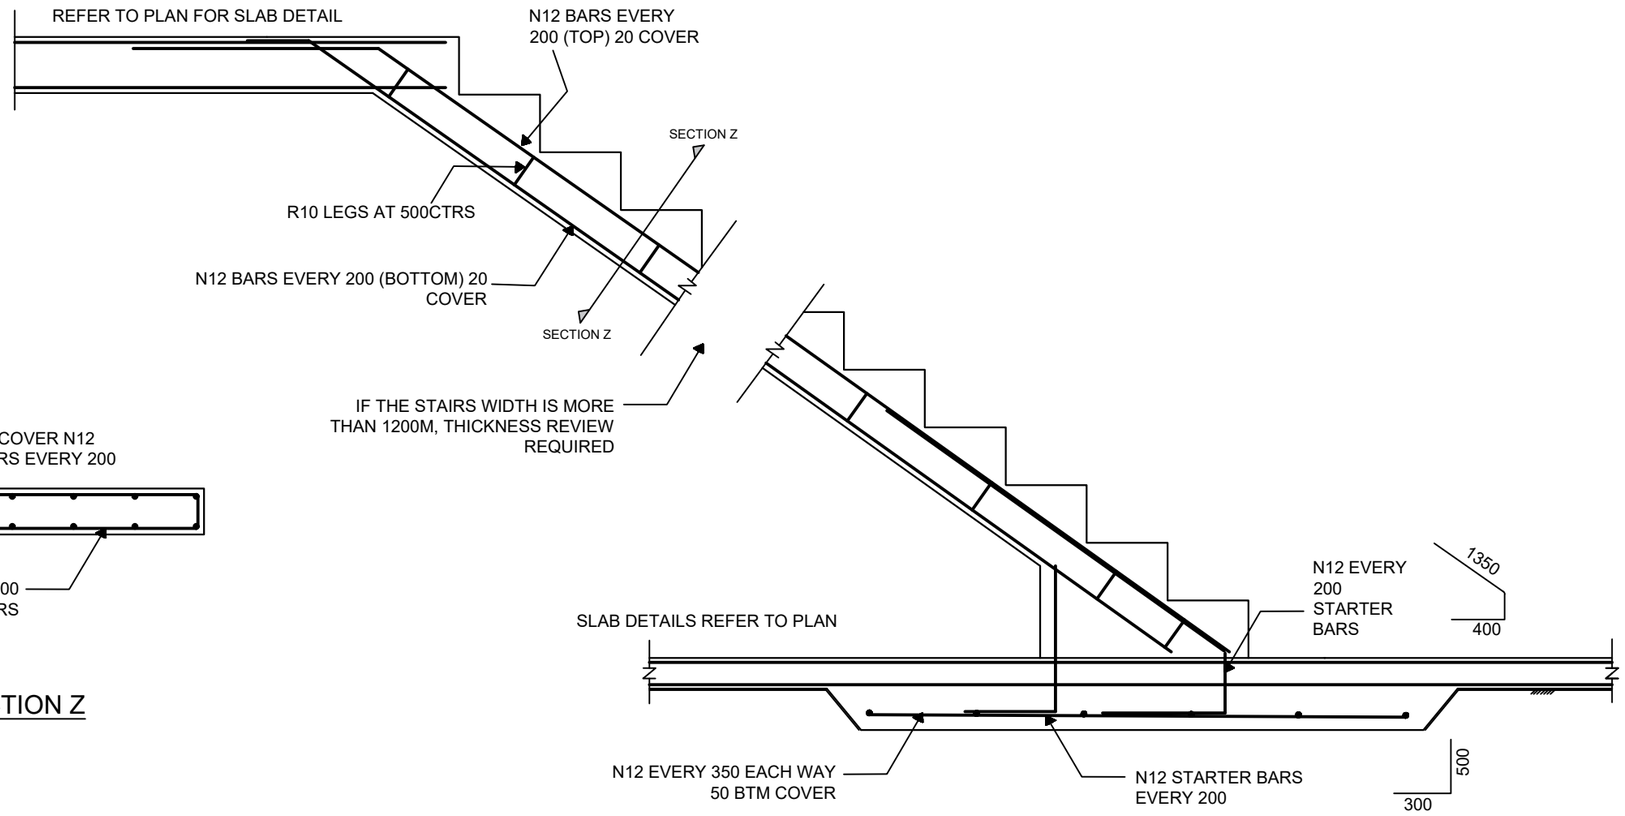

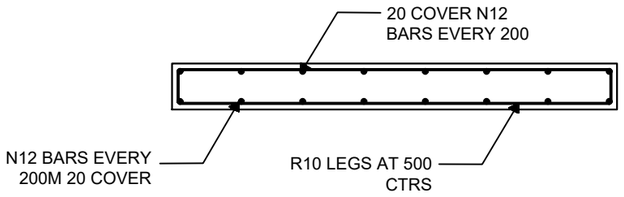


SECTION Z

RK INFRA
DESIGN | CONSULTING | DEVELOPMENT

Designed/Drawn	Checked	Council	PROJECT	DRAWING TITLE		NTS
M.HOSNI	A.ASHOSH	CANTERBURY BANKSTOWN	PROPOSED DUAL OCCUPANCY	STAIR DETAILS	26 LUCINDA AVENUE, BASS HILL, NSW	DRAWING NO. ST13
Approved K.NAJJAR	MOBILE 0414062484	Job No. 26LUC / Lot/DP 401/261279	Rev.No 02 / Publish Date 18/08/2026			


The contractor and / or subcontractors shall be responsible for all levels and dimensions prior to commencing on site or off site constructions and/or fabrications. These drawings must not be scaled. These drawings are dimensioned in (mms).These drawings must be read in conjunction with all other drawings and/or instructions as may be issued during the course of the project.These drawings are copyright and must not be retained, copied, developed or amended without a written consent from RK INFRA. All works resulting of these drawings are to be in accordance with 1- The Building Code of Australia. 2- All codes and regulations of LOCAL AUTHORITY REQUIREMENTS. 3- All related Trades Australian Standards. These drawings are site specific and can only be used for the address as listed in these drawings. These drawings are site specific and can only be used for the address listed in these drawings. 1. All works to be in accordance with the Building Code of Australia, Australian Standards, statutory regulations and local authority requirements. 2. Consistency between similar materials to be maintained. RK INFRA to be notified discrepancies, dimensional inconsistencies or the need for clarification prior to manufacture. 3. RK INFRA to approve all detailed drawings/setting out prior to construction.5. Contractors to confirm stability and feasibility of all units/components manufacture. 6. All drawing measurements to be verified on site - do not scale from documents. 7.Refer to this document in conjunction with Specification or any other plans such as structural, hydraulic and electrical (if applicable) for further information.

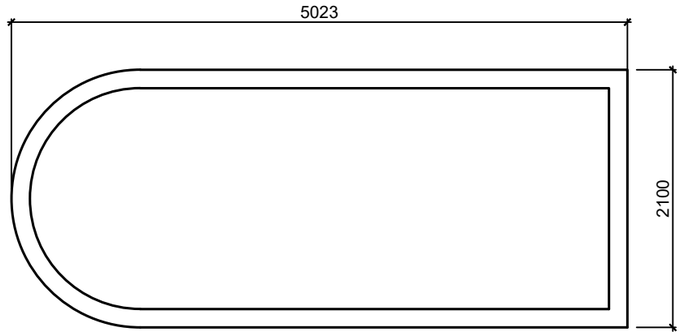

POOL LAYOUT PLAN

SCALE 1: 50


EXACT MEASUREMENT TO BE TAKEN FROM ARCHITECTURAL PLAN

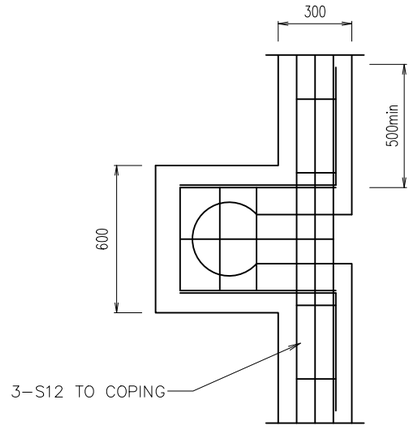

PLAN


SKIMMER DETAIL

SCALE 1: 20

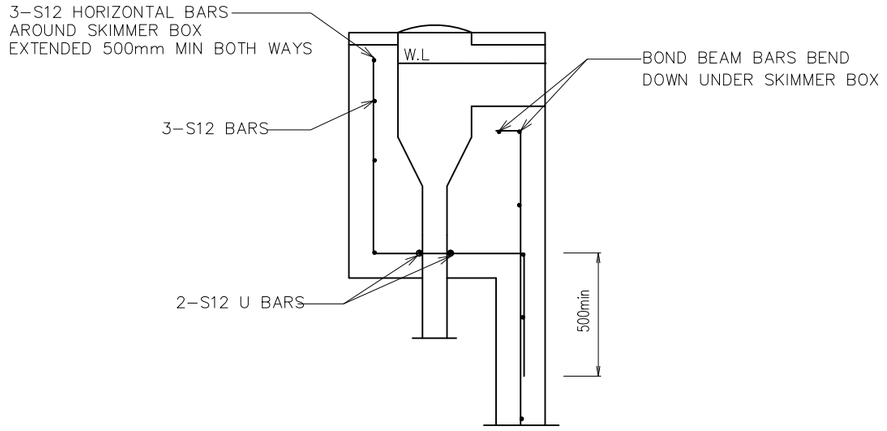

SECTION

SCALE 1: 20

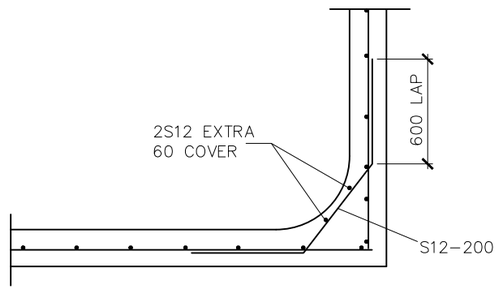

TYPICAL POOL CORNER DETAIL

SCALE 1: 20

FOUNDATION–SITE PREPARATION

SLAB DESIGN HAS BEEN DETAILED IN COMPLIANCE WITH AS 3600.

SOIL CLASSIFICATION SHALL BE CHECKED BY & CERTIFIED BY THE NOMINATED GEOTECHNICAL ENGINEER

POOL TO BE FOUNDED IN NATURAL CLAY FOUNDATION OF MINIMUM SAFE BEARING VALUE 400 KPa GEOTECHNICAL ENGINEER TO CONFIRM BEARING CAPACITY PRIOR TO CONCRETE PLACEMENT

STUCTURAL ENGINEEER TO BE CONTACTED IF SOIL CONDITIONS VARY.

ANY FILLING REQUIRED UNDER THE FLOOR SLAB SHALL CONSIST OF MATERIAL ACCEPTABLE TO THE GEOTECH ENGINEER AND COMPACTED IN LAYERS TO AS. 2870 SECTION 6

WPM– WATERPROOF MEMBRANE 0.2MM THICK POLYTHENE SHEETS WITH ALL JOINTS LAPPED MINIMUM 150MM AND TAPPED.

GENERAL NOTES

CONCRETE

ALL CONCRETE MATERIALS AND WORKMANSHIP TO BE IN ACCORDANCE WITH AS 3600 SAA CONCRETE STRUCTURES CODE – CURRENT EDITION.

PROVIDE CONCRETE WITH A MAXIMUM SLUMP OF 80MM TYPE A CEMENT,COURSE AGGREGATE MAXIMUM SIZE 20MM NO ADMIXTURES AND SHRINKAGE SHALL NOT EXCEED 630 MICRO STRAINS AT 56 DAYS.

CHARACTERISTIC CONCRETE COMPRESSIVE STRENGTH POOL MIX ON GROUND f'c=32MPa

CONCRETE IN SLABS TO BE FULLY COMPACTED BY HIGH FREQUENCY VIBRATOR.

CONCRETE SHALL BE CURED FOR AT LEAST 5 DAYS BY CONTINUOUS WATER SPRAY OR WEIGHTED PLASTIC MEMBRANE AND AT NO STAGE IS TO BECOME DRY.

CURING COMPOUNDS ARE ONLY TO BE UESD WHEN APPROVED BY THE ENGINEER.

REINFORCEMENT TO BE SUPPORTED ON BAR CHAIRS AND MAINTAINED IN POSITION SHOWN ON THE DRAWING

CHAIR SPACING SHALL NOT EXCEED 900MM FOR BARS AND 800MM FOR FABRIC.

ALL LAPPED SPLICES FOR STEEL FABRICS TO BE TWO OUTERMOST WIRES AND ONE FULL WIRE SPACING OF


COVER TO REO: SLAB 20 TOP 30 BOTTOM.

EACH SHEET.

RK INFRA
DESIGN | CONSULTING | DEVELOPMENT

Designed/Drawn	Checked	Council	PROJECT	DRAWING TITLE		AS SHOWN A3
M.HOSNI	A.ASHOSH	CANTERBURY BANKSTOWN	PROPOSED DUAL OCCUPANCY	POOL LAYOUT & DETAILS	26 LUCINDA AVENUE, BASS HILL, NSW	DRAWING NO. ST14
Approved	MOBILE	Job No.	Lot/DP	Rev.No	Publish Date	
K.NAJJAR	0414062484	26LUC	401/261279	02	18/08/2026	

The contractor and / or subcontractors shall be responsible for all levels and dimensions prior to commencing on site or off site constructions and/or fabrications. These drawings must not be scaled. These drawings are dimensioned in (mms).These drawings must be read in conjunction with all other drawings and/or instructions as may be issued during the course of the project.These drawings are copyright and must not be retained, copied, developed or amended without a written consent from RK INFRA. All works resulting of these drawings are to be in accordance with 1- The Building Code of Australia. 2- All codes and regulations of LOCAL AUTHORITY REQUIREMENTS. 3- All related Trades Australian Standards. These drawings are site specific and can only be used for the address as listed in these drawings. These drawings are site specific and can only be used for the address listed in these drawings. 1. All works to be in accordance with the Building Code of Australia, Australian Standards, statutory regulations and local authority requirements. 2. Consistency between similar materials to be maintained. RK INFRA to be notified discrepancies, dimensional inconsistencies or the need for clarification prior to manufacture. 3. RK INFRA to approve all detailed drawings/setting out prior to construction.5. Contractors to confirm stability and feasibility of all units/components manufacture. 6. All drawing measurements to be verified on site - do not scale from documents. 7.Refer to this document in conjunction with Specification or any other plans such as structural, hydraulic and electrical (if applicable) for further information.

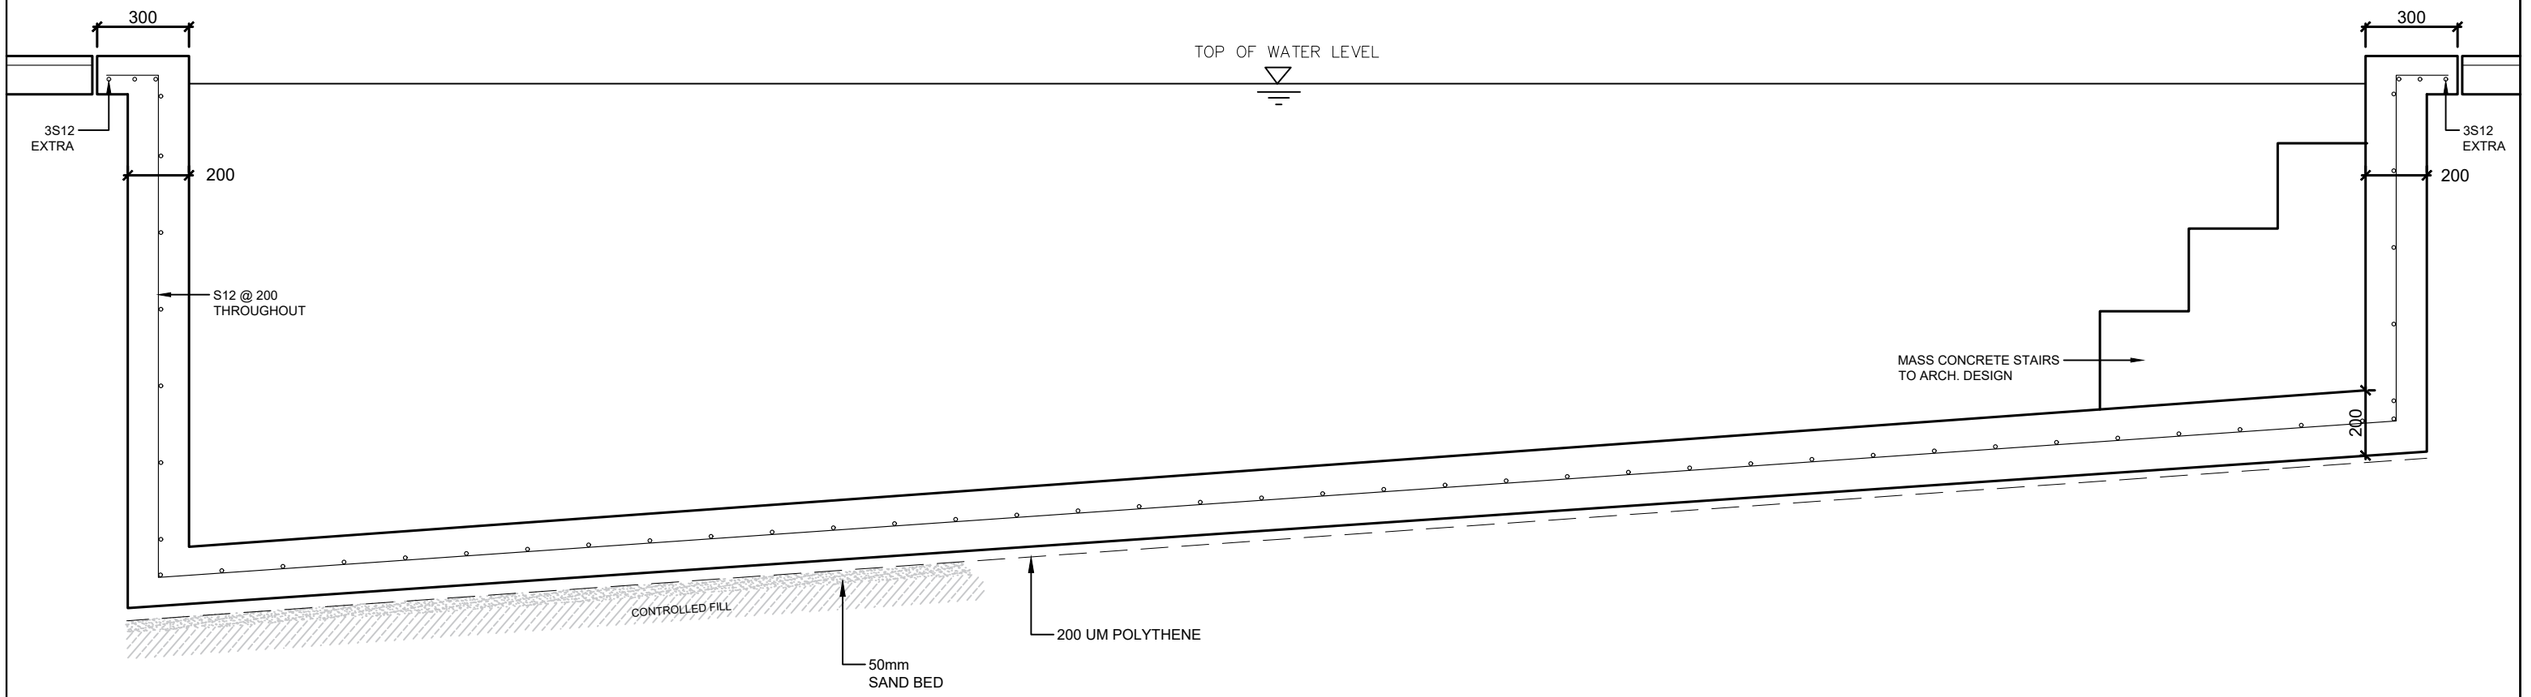

LONGITUDINAL SECTION


NTS

EXACT GEOMETRY & MEASUREMENT TO BE TAKEN FROM ARCHITECTURAL PLAN

RK INFRA
DESIGN | CONSULTING | DEVELOPMENT

Designed/Drawn M.HOSNI	Checked A.ASHOSH	Council CANTERBURY BANKSTOWN		PROJECT PROPOSED DUAL OCCUPANCY		DRAWING TITLE POOL SECTION	NTS
Approved K.NAJJAR	MOBILE 0414062484	Job No. 26LUC	Lot/DP 401/261279	Rev.No 02	Publish Date 18/08/2026	26 LUCINDA AVENUE, BASS HILL, NSW	DRAWING NO. ST15

The contractor and / or subcontractors shall be responsible for all levels and dimensions prior to commencing on site or off site constructions and/or fabrications. These drawings must not be scaled. These drawings are dimensioned in (mms).These drawings must be read in conjunction with all other drawings and/or instructions as may be issued during the course of the project.These drawings are copyright and must not be retained, copied, developed or amended without a written consent from RK INFRA. All works resulting of these drawings are to be in accordance with 1- The Building Code of Australia. 2- All codes and regulations of LOCAL AUTHORITY REQUIREMENTS. 3- All related Trades Australian Standards. These drawings are site specific and can only be used for the address as listed in these drawings. These drawings are site specific and can only be used for the address listed in these drawings. 1. All works to be in accordance with the Building Code of Australia, Australian Standards, statutory regulations and local authority requirements. 2. Consistency between similar materials to be maintained. RK INFRA to be notified discrepancies, dimensional inconsistencies or the need for clarification prior to manufacture. 3. RK INFRA to approve all detailed drawings/setting out prior to construction.5. Contractors to confirm stability and feasibility of all units/components manufacture. 6. All drawing measurements to be verified on site - do not scale from documents. 7.Refer to this document in conjunction with Specification or any other plans such as structural, hydraulic and electrical (if applicable) for further information.

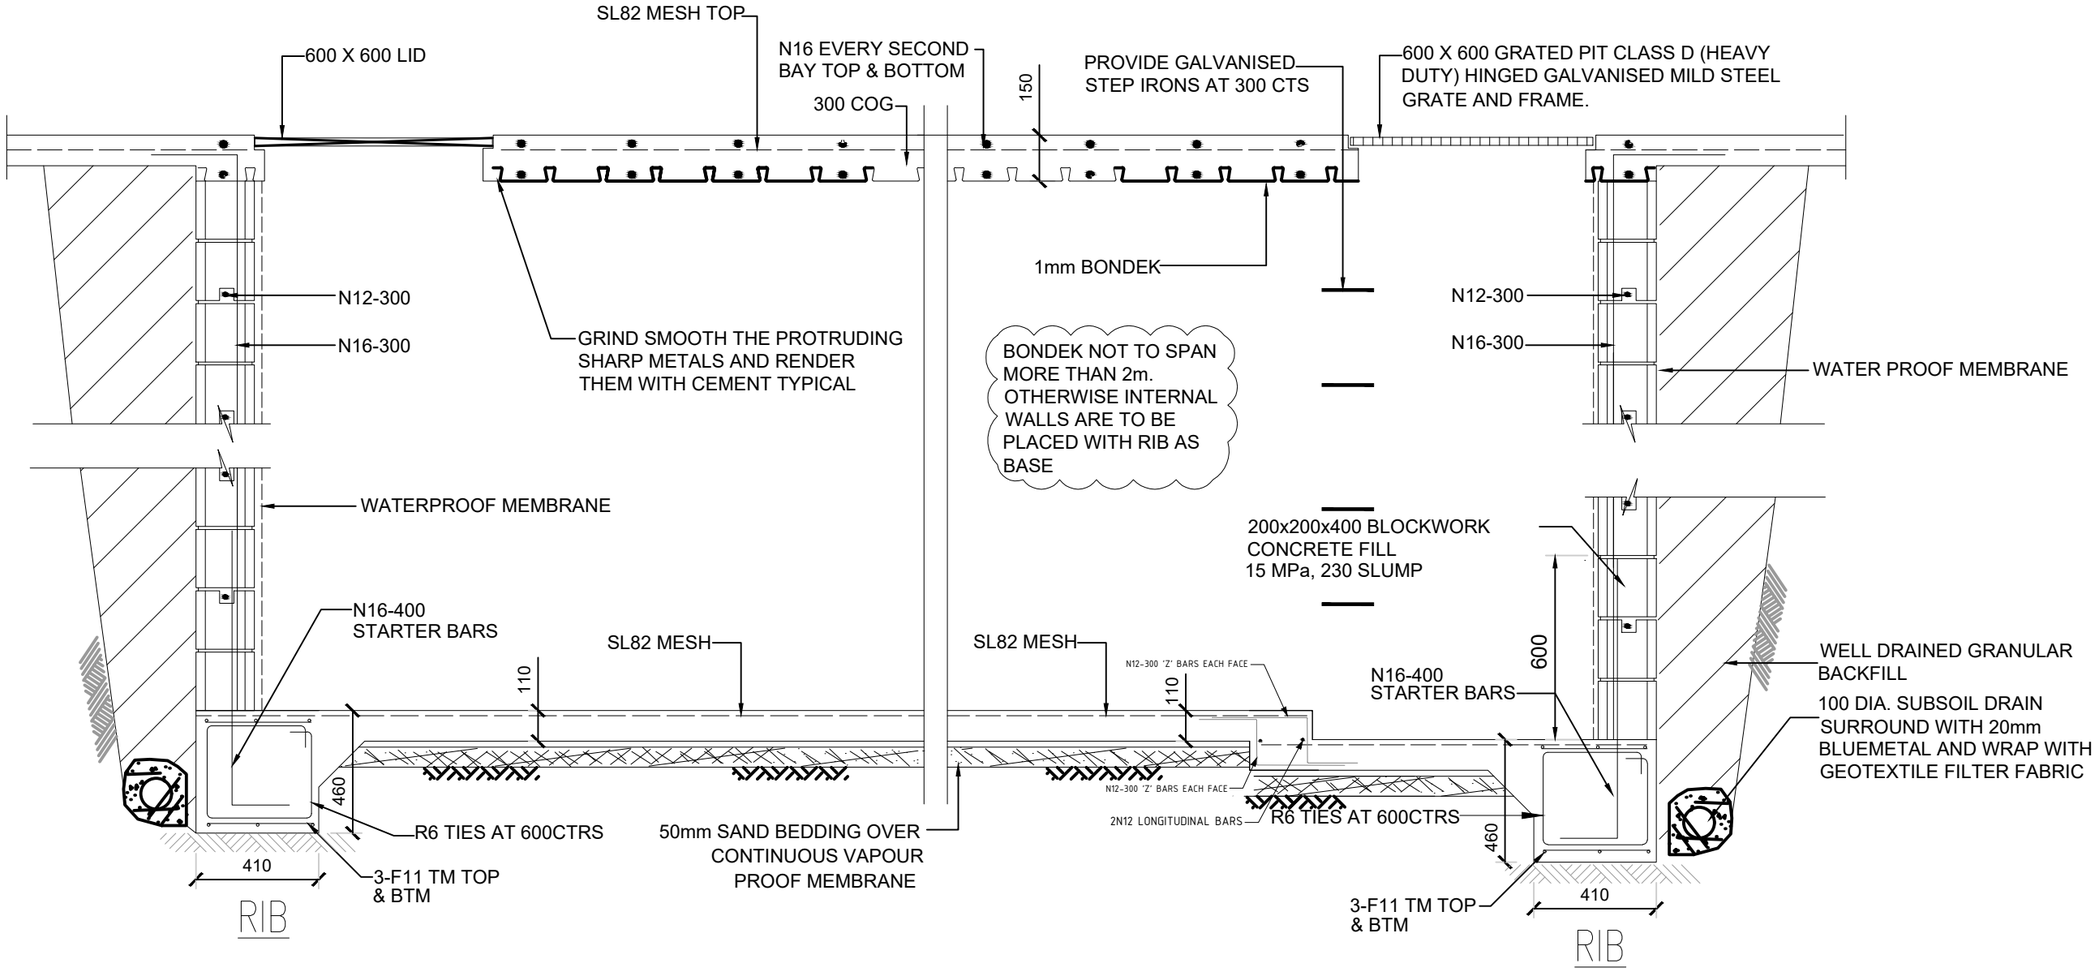

IN GROUND TANK DETAIL (OSD)

RK INFRA
DESIGN | CONSULTING | DEVELOPMENT

Designed/Drawn M.HOSNI	Checked A.ASHOSH	Council CANTERBURY BANKSTOWN	PROJECT PROPOSED DUAL OCCUPANCY	DRAWING TITLE OSD DETAIL	26 LUCINDA AVENUE, BASS HILL, NSW	NTS
Approved K.NAJJAR	MOBILE 0414062484	Job No. 26LUC / Lot/DP 401/261279	Rev.No 02 / Publish Date 18/08/2026			DRAWING NO. ST16

The contractor and / or subcontractors shall be responsible for all levels and dimensions prior to commencing on site or off site constructions and/or fabrications. These drawings must not be scaled. These drawings are dimensioned in (mms).These drawings must be read in conjunction with all other drawings and/or instructions as may be issued during the course of the project.These drawings are copyright and must not be retained, copied, developed or amended without a written consent from RK INFRA. All works resulting of these drawings are to be in accordance with 1- The Building Code of Australia. 2- All codes and regulations of LOCAL AUTHORITY REQUIREMENTS. 3- All related Trades Australian Standards. These drawings are site specific and can only be used for the address as listed in these drawings. These drawings are site specific and can only be used for the address listed in these drawings. 1. All works to be in accordance with the Building Code of Australia, Australian Standards, statutory regulations and local authority requirements. 2. Consistency between similar materials to be maintained. RK INFRA to be notified discrepancies, dimensional inconsistencies or the need for clarification prior to manufacture. 3. RK INFRA to approve all detailed drawings/setting out prior to construction.5. Contractors to confirm stability and feasibility of all units/components manufacture. 6. All drawing measurements to be verified on site - do not scale from documents. 7.Refer to this document in conjunction with Specification or any other plans such as structural, hydraulic and electrical (if applicable) for further information.