257 MARSDEN ROAD, CARLINGFORD NSW 2118
DUAL OCCUPANCY DA APPLICATION

DA DOCUMENTATION SUBMISSION

DRAWING LIST

DRAWING NO	TITLE	REV	DATE
A000	COVER SHEET & LOCATION PLAN	C	29/07/26
A002	BASIX COMMITMENTS	C	29/07/26
A003	DEMOLITION PLAN	C	29/07/26
A004	PROPOSED SUBDIVISION PLAN	C	29/07/26
A005	CUT AND FILL PLAN	C	29/07/26
A100	PROPOSED SITE PLAN	C	29/07/26
A201	PROPOSED GROUND FLOOR PLAN	C	29/07/26
A205	PROPOSED FIRST FLOOR PLAN	C	29/07/26
A206	PROPOSED ROOF PLAN	C	29/07/26
A300	FINISHED MATERIAL BOARD	C	29/07/26
A301	SOUTH ELEVATION	C	29/07/26
A302	NORTH ELEVATION	C	29/07/26
A303	EAST ELEVATION	C	29/07/26
A304	WEST ELEVATION	C	29/07/26

DRAWING LIST

DRAWING NO	TITLE	REV	DATE
A305	SOUTH FENCE ELEVATION	C	29/07/26
A401	PROPOSED SECTION A	C	29/07/26
A402	PROPOSED SECTION B	C	29/07/26
A411	WINDOW AND DOOR SCHEDULE	C	29/07/26
A420	CONSTRUCTION MANAGEMENT PLAN	C	29/07/26
A421	WASTE MANAGEMENT PLAN	C	29/07/26
A500	GFA DIAGRAM	C	29/07/26
A501	LANDSCAPE DIAGRAM	C	29/07/26
A502	EXISTING SHADOW DIAGRAM	C	29/07/26
A503	PROPOSED SHADOW DIAGRAM	C	29/07/26
A510	EXISTING SOLAR DIAGRAM	C	29/07/26
A511	PROPOSED SOLAR DIAGRAM	C	29/07/26
A602	PROPOSED PERSPECTIVE	C	29/07/26
A603	PROPOSED PERSPECTIVE 2	C	29/07/26



LOCATION PLAN

NOTES

- ALL WORKS TO BE IN ACCORDANCE WITH THE BUILDING CODE OF AUSTRALIA, AUSTRALIAN STANDARDS, STATUTORY REGULATIONS AND LOCAL AUTHORITY REQUIREMENTS.
- CONTRACTOR TO ENSURE CONSISTENCY BETWEEN SIMILAR MATERIAL IS MAINTAINED.
- PREPARE & MAKE GOOD ALL SURFACES & SUBSTRATE AS REQUIRED TO RECEIVE NEW FINISHES AS PER MANUFACTURER'S SPECIFICATION.
- ALL DIMENSIONS TO BE CHECKED ON SITE BEFORE COMMENCEMENT OF WORK. ALL DIMENSIONS MUST BE CHECKED & VERIFIED ON SITE PRIOR TO CONSTRUCTION & MANUFACTURE OF ANY ITEM.
- THIS DRAWING IS COPYRIGHT AND THE PROPERTY OF THE AUTHOR. IT MUST NOT BE RETAINED, COPIED OR USED WITHOUT THE EXPRESS AUTHORITY OF PLAY CO PTY LTD.

REV	DATE	DESCRIPTION
P1	19/09/25	PRELIMINARY PLAN
P2	08/12/25	PRELIMINARY PLAN
P3	21/01/26	PRELIMINARY PLAN
A	17/02/26	DA SUBMISSION
B	10/07/26	RFI
C	29/07/26	RFI

PROJECT
257 MARSDEN ROAD CARLINGFORD

ARCHITECT

PLAY CO ARCHITECTS
ARCHITECTURE | INTERIORS | PROJECT MANAGEMENT
PLAY CO PTY LTD
ABN 206 135 521 86
SUITE 801, 11 HELP STREET
CHATSWOOD NSW 2067
WWW.PLAY-CO.COM.AU
NOMINATED ARCHITECT
RAYMOND NG #8961
DESIGN PRACTITIONER DEP000234

CLIENT

PROJECT NUMBER	P632	PROJECT ADDRESS	257 MARSDEN ROAD CARLINGFORD		
DRAWING NUMBER	A000	DRAWING TITLE	COVER SHEET & LOCATION PLAN		
SCALE		PAPER SIZE	A3	REVISION	C
DRAWN BY	TT	REVIEWED BY	RN	STATUS	RFI



Nationwide House Energy Rating Scheme®
Multiple Class 1 Dwellings Summary
NatHERS® Certificate No. XJ4BUJSQDQ

Generated on 18 Feb 2026 using FirstRate5 v5.5.5a

Property

Address	257 Marsden Road, Carlingford, NSW, 2118
Lot/DP	
NatHERS Climate Zone	Mascot (Sydney Airport)

Accredited assessor

Name	Dimitrios Harakidas
Business name	AENEC
Email	info@aenec.com.au
Phone	0416316204
Accreditation No.	HERA10042
Assessor Accrediting Organisation	HERA

Verification

To verify this certificate, scan the QR code or visit https://www.fr5.com.au/QRCodeLanding?PublicId=XJ4BUJSQDQ&GrpCan=1
When using either link, ensure you are visiting www.fr5.com.au.

National Construction Code (NCC) requirements

The NCC allows the use of NatHERS accredited software to comply with the energy efficiency requirements for houses (Class 1 buildings) and apartments (Class 2 sole-occupancy units and Class 4 parts of buildings). The applicable requirements for houses are detailed in Specification 42 of NCC Volume Two. For apartments the requirements are detailed in clauses J3D3 and J3D15 of NCC Volume One.

NCC 2022 includes enhanced thermal performance requirements for houses and apartments. It also includes a new whole-of-home annual energy use budget which applies to the major equipment in the home.

The NCC, and associated ABCB Standards and support material, can be accessed at www.abcb.gov.au.

Note, variations and additions to the NCC energy efficiency requirements may apply in some states and territories.

Summary of all dwellings

Certificate number and link	Unit number	Heating load (load limit) [MJ/m²/p.a.]	Cooling load (load limit) [MJ/m²/p.a.]	Total load [MJ/m²/p.a.]	Star rating	Whole of Home Rating
Q2JVCIFBJM	257	16.2 (N/A)	13.2 (N/A)	29.4	7.1	NA
5OCNQKZ34P	257A	15.9 (N/A)	13.5 (N/A)	29.4	7.1	NA

Nationwide House Energy Rating Scheme (NatHERS) is an initiative of the Australian, state and territory governments. For more details see www.nathers.gov.au.
Generated on 18 Feb 2026 using FirstRate5 v5.5.5a for 257 Marsden Road, Carlingford, NSW, 2118

Nationwide House Energy Rating Scheme®
NatHERS® Certificate No. 5OCNQKZ34P

Generated on 18 Feb 2026 using FirstRate5: 5.5.5a (3.22)

Property

Address	257A, 257 Marsden Road, Carlingford, NSW, 2118
Lot/DP	4/217529
NCC Class*	Class 1a
Floor/all Floors Type	New Home

Plans

Main plan	P632 Rev. A 17.2.2026
Prepared by	Play Co Architects

Construction and environment

Assessed floor area [m²]*		Exposure type
Conditioned*	215	suburban
Unconditioned*	30.6	**NatHERS climate zone**
Total	245.6	56 Mascot AMO
Garage	17.7	

Accredited assessor

Name	Dimitrios Harakidas
Business name	AENEC
Email	info@aenec.com.au
Phone	0416316204
Accreditation No.	HERA10042
Assessor Accrediting Organisation	HERA
Declaration of interest	No

NCC Requirements

NCC provisions	Volume 2
State/Territory variation	Yes

National Construction Code (NCC) requirements

The NCC allows the use of NatHERS accredited software to comply with the energy efficiency requirements for houses (Class 1 buildings) and apartments (Class 2 sole-occupancy units and Class 4 parts of buildings). The applicable requirements for houses are detailed in Specification 42 of NCC Volume Two. For apartments the requirements are detailed in clauses J3D3 and J3D15 of NCC Volume One.

NCC 2022 includes enhanced thermal performance requirements for houses and apartments. It also includes a new whole-of-home annual energy use budget which applies to the major equipment in the home.

The NCC, and associated ABCB Standards and support material, can be accessed at www.abcb.gov.au.

Note, variations and additions to the NCC energy efficiency requirements may apply in some states and territories.

Thermal performance star rating



Thermal performance [MJ/m²]

Limits taken from ABCB Standard 2022

	Heating	Cooling
Modelled	15.9	13.5
Load limits	N/A	N/A

Features determining load limits

Floor type (lowest conditioned area)	N/A
NCC climate zone 1 or 2	N/A
Outdoor living area	N/A
Outdoor living area ceiling fan	N/A

Whole of Home performance rating

No Whole of Home performance rating generated for this certificate

Verification

To verify this certificate, scan the QR code or visit https://www.fr5.com.au/QRCodeLanding?PublicId=5OCNQKZ34P
When using either link, ensure you are visiting www.fr5.com.au.

*Refer to glossary.
Generated on 18 Feb 2026 using FirstRate5: 5.5.5a (3.22) for 4/217529, 257A, 257 Marsden Road, Carlingford, NSW, 2118

Nationwide House Energy Rating Scheme®
NatHERS® Certificate No. Q2JVCIFBJM

Generated on 18 Feb 2026 using FirstRate5: 5.5.5a (3.22)

Property

Address	257, 257 Marsden Road, Carlingford, NSW, 2118
Lot/DP	4/217529
NCC Class*	Class 1a
Floor/all Floors Type	New Home

Plans

Main plan	P632 Rev. A 17.2.2026
Prepared by	Play Co Architects

Construction and environment

Assessed floor area [m²]*		Exposure type
Conditioned*	215	suburban
Unconditioned*	30.6	**NatHERS climate zone**
Total	245.6	56 Mascot AMO
Garage	17.7	

Accredited assessor

Name	Dimitrios Harakidas
Business name	AENEC
Email	info@aenec.com.au
Phone	0416316204
Accreditation No.	HERA10042
Assessor Accrediting Organisation	HERA
Declaration of interest	No

NCC Requirements

NCC provisions	Volume 2
State/Territory variation	Yes

National Construction Code (NCC) requirements

The NCC allows the use of NatHERS accredited software to comply with the energy efficiency requirements for houses (Class 1 buildings) and apartments (Class 2 sole-occupancy units and Class 4 parts of buildings). The applicable requirements for houses are detailed in Specification 42 of NCC Volume Two. For apartments the requirements are detailed in clauses J3D3 and J3D15 of NCC Volume One.

NCC 2022 includes enhanced thermal performance requirements for houses and apartments. It also includes a new whole-of-home annual energy use budget which applies to the major equipment in the home.

The NCC, and associated ABCB Standards and support material, can be accessed at www.abcb.gov.au.

Note, variations and additions to the NCC energy efficiency requirements may apply in some states and territories.

Thermal performance star rating



Thermal performance [MJ/m²]

Limits taken from ABCB Standard 2022

	Heating	Cooling
Modelled	16.2	13.2
Load limits	N/A	N/A

Features determining load limits

Floor type (lowest conditioned area)	N/A
NCC climate zone 1 or 2	N/A
Outdoor living area	N/A
Outdoor living area ceiling fan	N/A

Whole of Home performance rating

No Whole of Home performance rating generated for this certificate

Verification

To verify this certificate, scan the QR code or visit https://www.fr5.com.au/QRCodeLanding?PublicId=Q2JVCIFBJM
When using either link, ensure you are visiting www.fr5.com.au.

*Refer to glossary.
Generated on 18 Feb 2026 using FirstRate5: 5.5.5a (3.22) for 4/217529, U 257, 257 Marsden Road, Carlingford, NSW, 2118

BASIX™ Certificate

Building Sustainability Index
www.planningportal.nsw.gov.au/development-and-assessment/basix

Multi Dwelling

Certificate number: 1855764M

This certificate confirms that the proposed development will meet the NSW government's requirements for sustainability, if it is built in accordance with the commitments set out below. Terms used in this certificate, or in the commitments, have the meaning given by the document entitled "BASIX Definitions" dated 10/08/2020 published by the Department. This document is available at www.planningportal.nsw.gov.au/definitions

Secretary
Date of issue: Wednesday, 18 February 2026
To be valid, this certificate must be submitted with a development application or lodged with a complying development certificate application within 3 months of the date of issue.

NSW

When submitting this BASIX certificate with a development application or complying development certificate application, it must be accompanied by NatHERS certificate XJ4BUJSQDQ.

Project summary	
Project name	257 Marsden Road Carlingford
Street address	257 MARSDEN ROAD CARLINGFORD 2118
Local Government Area	CITY OF PARRAMATTA
Plan type and plan number	Deposited Plan 217529
Lot No.	4
Section no.	
No. of residential flat buildings	0
Residential flat buildings: no. of dwellings	0
Multi-dwelling housing: no. of dwellings	2
No. of single dwelling houses	0

Project score		
Water	✔ 40	Target 40
Thermal Performance	✔ Pass	Target Pass
Energy	✔ 74	Target 72
Materials	✔ -68	Target n/a

Certificate Prepared by
Name / Company Name: AENEC - Office: 02 9994 8906
ABN (if applicable): 32612556377

Description of project

Project address	
Project name	257 Marsden Road Carlingford
Street address	257 MARSDEN ROAD CARLINGFORD 2118
Local Government Area	CITY OF PARRAMATTA
Plan type and plan number	Deposited Plan 217529
Lot No.	4
Section no.	
Project type	
No. of residential flat buildings	0
Residential flat buildings: no. of dwellings	0
Multi-dwelling housing: no. of dwellings	2
No. of single dwelling houses	0
Site details	
Site area (m²)	942.2
Roof area (m²)	216.2
Non-residential floor area (m²)	
Residential car spaces	0
Non-residential car spaces	

Common area landscape	
Common area lawn (m²)	0
Common area garden (m²)	0
Area of indigenous or low water use species (m²)	0
Assessor details and thermal loads	
Assessor number	HERA10042
Certificate number	XJ4BUJSQDQ
Climate zone	56
Project score	
Water	✔ 40 — Target 40
Thermal Performance	✔ Pass — Target Pass
Energy	✔ 74 — Target 72
Materials	✔ -68 — Target n/a

Schedule of BASIX commitments

The commitments set out below regulate how the proposed development is to be carried out. It is a condition of any development consent granted, or complying development certificate issued, for the proposed development, that BASIX commitments be complied with.

1. Commitments for multi-dwelling housing

(a) Dwellings

(i) Water	Show on DA plans	Show on CC/CDC plans & specs	Certifier check
(a) The applicant must comply with the commitments listed below in carrying out the development of a dwelling listed in a table below.			
(b) The applicant must plant indigenous or low water use species of vegetation throughout the area of land specified for the dwelling in the "Indigenous species" column of the table below, as private landscaping for that dwelling. (This area of indigenous vegetation is to be contained within the "Area of garden and lawn" for the dwelling specified in the "Description of Project" table).	✔	✔	
(c) If a rating is specified in the table below for a fixture or appliance to be installed in the dwelling, the applicant must ensure that each such fixture and appliance meets the rating specified for it.		✔	✔
(d) The applicant must install an on-demand hot water recirculation system which regulates all hot water use throughout the dwelling, where indicated for a dwelling in the "HW recirculation or diversion" column of the table below.		✔	✔
(e) The applicant must install:			
(aa) a hot water diversion system to all showers, kitchen sinks and all basins in the dwelling, where indicated for a dwelling in the "HW recirculation or diversion" column of the table below; and		✔	✔
(bb) a separate diversion tank (or tanks) connected to the hot water diversion systems of at least 100 litres. The applicant must connect the hot water diversion tank to all toilets in the dwelling.		✔	✔
(e) The applicant must not install a private swimming pool or spa for the dwelling, with a volume exceeding that specified for it in the table below.	✔	✔	
(f) If specified in the table, that pool or spa (or both) must have a pool cover or shading (or both).		✔	
(g) This pool or spa must be located as specified in the table.	✔	✔	
(h) The applicant must install, for the dwelling, each alternative water supply system, with the specified size, listed for that dwelling in the table below. Each system must be configured to collect run-off from the areas specified (excluding any area which supplies any other alternative water supply system), and to divert overflow as specified. Each system must be connected as specified.	✔	✔	✔

Fixtures						Appliances		Individual pool				Individual spa		
Dwelling no.	All shower-heads	All toilet flushing systems	All kitchen taps	All bathroom taps	HW recirculation or diversion	All clothes washers	All dish-washers	Volume (kL)	Pool cover	Pool location	Pool shaded	Volume (kL)	Spa cover	Spa shaded
All dwellings	4 star (> 4.5 but <= 6 L/min)	4 star	4 star	4 star	-	-	-	-	-	-	-	-	-	-

Alternative water source								
Dwelling no.	Alternative water supply systems	Size	Configuration	Landscape connection	Toilet connection	Laundry connection	Pool top-up	Spa top-up
All dwellings	Individual water tank (No. 1)	Tank size (min) 2000 litres	To collect run-off from at least: 120 square metres of roof area; 0.00 square metres of impervious area; 0.00 square metres of garden and lawn area; and, 0.00 square metres of planter box area.	yes	no	yes	no	no

(ii) Energy	Show on DA plans	Show on CC/CDC plans & specs	Certifier check
(a) The applicant must comply with the commitments listed below in carrying out the development of a dwelling listed in a table below.			
(b) The applicant must install each hot water system specified for the dwelling in the table below, so that the dwelling's hot water is supplied by that system. If the table specifies a central hot water system for the dwelling, then the applicant must connect that central system to the dwelling, so that the dwelling's hot water is supplied by that central system.	✔	✔	✔
(c) The applicant must install, in each bathroom, kitchen and laundry of the dwelling, the ventilation system specified for that room in the table below. Each such ventilation system must have the operation control specified for it in the table.		✔	✔
(d) The applicant must install the cooling and heating systems specified for the dwelling under the "Living areas" and "Bedroom areas" columns in the table below. If no system is specified in these columns, or if at least 1 living/bedroom area of the dwelling, if no cooling or heating system is specified in the table for "Living areas" or "Bedroom areas", then no systems may be installed in any such areas. If the term "zoned" is specified beside an air conditioning system, then the system must provide for day/night zoning between living areas and bedrooms.		✔	✔
(e) This commitment applies to each room or area of the dwelling which is referred to in a heading to the "Artificial lighting" column of the table below (but only to the extent specified for that room or area). The applicant must ensure that the "primary type of artificial lighting" for each such room in the dwelling is fluorescent lighting or light emitting diode (LED) lighting. If the term "dedicated" is specified for a particular room or area, then the light fittings in that room or area must only be capable of being used for fluorescent lighting or light emitting diode (LED) lighting.		✔	✔

(iii) Thermal Performance and Materials	Show on DA plans	Show on CC/CDC plans & specs	Certifier check
(aa) Install insulation with an R-value of not less than 1.0 around the vertical edges of the perimeter of the slab; or			
(bb) On a suspended floor, install insulation with an R-value of not less than 1.0 underneath the slab and around the vertical edges of the perimeter of the slab.			
(h) The applicant must construct the floors and walls of this development in accordance with the specifications listed in the table below.	✔	✔	✔
(i) The applicant must show on the plans accompanying The development application for The proposed development. The locations of ceiling fans set out in The Assessor Certificate.	✔		
(j) The applicant must show on the plans accompanying the application for a construction certificate (or complying development certificate, if applicable), the locations of ceiling fans set out in the Assessor Certificate.		✔	

Thermal loads		
Dwelling no.	Area adjusted heating load (in MJ/m²/yr)	Area adjusted cooling load (in MJ/m²/yr)	Area adjusted total load (in MJ/m²/yr)
257	16.2	13.2	29.400
All other dwellings	15.9	13.5	29.400

Construction of floors and walls						
Dwelling no.	Concrete slab on ground (m²)	Suspended floor with open subfloor (m²)	Suspended floor with enclosed subfloor (m²)	Suspended floor above garage (m²)	Primarily rammed earth or mudbrick walls	
All dwellings	110.4	4.1	-	17.7	no	

Floor types											
	Concrete slab on ground			Suspended floor above enclosed subfloor			Suspended floor above open subfloor				
Dwelling no.	Area (m²)	Insulation	Low emissions option	Elevated/insulation	Construction type	Area (m²)	Insulation	Construction type	Area (m²)	Insulation
All dwellings	110.4	-	-	conventional slab	-	-	-	44C panel (75 mm) - concrete - timber - untreated softwood	4.1	fibreglass batts or roll

(iv) Energy	Show on DA plans	Show on CC/CDC plans & specs	Certifier check
(i) This commitment applies to each room or area of the dwelling which is referred to in a heading to the "Natural lighting" column of the table below (but only to the extent specified for that room or area). The applicant must ensure that each such room or area is fitted with a window and/or skylight.	✔	✔	✔
(ii) This commitment applies if the applicant installs a water heating system for the dwelling's pool or spa. The applicant must:			
(aa) install the system specified for the pool in the "Individual Pool" column of the table below (or alternatively must not install any system for the pool). If specified, the applicant must install a timer, to control the pool's pump; and		✔	
(bb) install the system specified for the spa in the "Individual Spa" column of the table below (or alternatively must not install any system for the spa). If specified, the applicant must install a timer to control the spa's pump.		✔	
(v) The applicant must install in the dwelling:			
(aa) the kitchen cook-top and oven specified for that dwelling in the "Appliances & other efficiency measures" column of the table below;		✔	
(bb) each appliance for which a rating is specified for that dwelling in the "Appliances & other efficiency measures" column of the table, and ensure that the appliance has that minimum rating; and		✔	✔
(cc) any clothes drying line specified for the dwelling in the "Appliances & other efficiency measures" column of the table.		✔	
(i) If specified in the table, the applicant must carry out the development so that each refrigerator space in the dwelling is "well ventilated".		✔	
(j) The applicant must install the photovoltaic system specified for the dwelling under the "Photovoltaic system" heading of the "Alternative energy" column of the table below, and connect the system to that dwelling's electrical system.	✔	✔	✔

Hot water		Bathroom ventilation system		Kitchen ventilation system		Laundry ventilation system	
Dwelling no.	Hot water system	Each bathroom	Operation control	Each kitchen	Operation control	Each laundry	Operation control
All dwellings	gas instantaneous - 6 star	individual fan, ducted to façade or roof	manual switch on/off	individual fan, ducted to façade or roof	manual switch on/off	natural ventilation only, or no laundry	

Cooling		Heating		Natural lighting	
Dwelling no.	living areas	bedroom areas	living areas	bedroom areas	No. of bathrooms or toilets	Main kitchen
All dwellings	1-phase airconditioning - ducted - 3 star (average zone)	1-phase airconditioning - ducted - 3 star (average zone)	1-phase airconditioning - ducted - 3 star (average zone)	1-phase airconditioning - ducted - 3 star (average zone)	3	yes

2. Commitments for common areas and central systems/facilities for the development (non-building specific)

(b) Common areas and central systems/facilities

(i) Water	Show on DA plans	Show on CC/CDC plans & specs	Certifier check
(a) If, in carrying out the development, the applicant installs a showerhead, toilet, tap or clothes washer into a common area, then that item must meet the specifications listed for it in the table.		✔	✔
(b) The applicant must install (or ensure that the development is serviced by) the alternative water supply system(s) specified in the "Central systems" column of the table below. In each case, the system must be sized, be configured, and be connected, as specified in the table.	✔	✔	✔
(c) A swimming pool or spa listed in the table must not have a volume (in kL) greater than that specified for the pool or spa in the table.	✔	✔	
(d) A pool or spa listed in the table must have a cover or shading if specified for the pool or spa in the table.		✔	
(e) The applicant must install each fire sprinkler system listed in the table so that the system is configured as specified in the table.		✔	✔
(f) The applicant must ensure that the central cooling system for a cooling tower is configured as specified in the table.		✔	✔

Common areas	Showerheads rating	Toilets rating	Taps rating	Clothes washers rating
All common areas	no common facility	no common facility	no common facility	no common laundry facility

(ii) Energy	Show on DA plans	Show on CC/CDC plans & specs	Certifier check
(a) If, in carrying out the development, the applicant installs a ventilation system to service a common area specified in the table below, then that ventilation system must be of the type specified for that common area, and must meet the efficiency measure specified.		✔	✔
(b) In carrying out the development, the applicant must install, as the "primary type of artificial lighting" for each common area specified in this table below, the lighting specified for that common area. This lighting must meet the efficiency measure specified. The applicant must also install a centralised lighting control system or Building Management System (BMS) for the common area, where specified.		✔	✔
(c) The applicant must install the systems and fixtures specified in the "Central energy systems" column of the table below. In each case, the system or fixture must be of the type, and meet the specifications, listed for it in the table.	✔	✔	✔

Central energy systems	Type	Specification
Other	-	

Alternative energy			
Dwelling no.	Photovoltaic system (min rated electrical output in peak kW)	Photovoltaic collector installation	Orientation Inputs
All dwellings			

(iii) Thermal Performance and Materials	Show on DA plans	Show on CC/CDC plans & specs	Certifier check
(a) The applicant must attach the certificate referred to under "Assessor details" on the front page of this BASIX certificate (the "Assessor Certificate") to the development application and construction certificate application for the proposed development (or, if the applicant is applying for a complying development certificate for the proposed development, to that application). The applicant must also attach the Assessor Certificate to the application for a final occupation certificate for the proposed development.			
(b) The Assessor Certificate must have been issued by an Accredited Assessor in accordance with the Thermal Comfort Protocol.			
(c) The details of the proposed development on the Assessor Certificate must be consistent with the details shown in this BASIX Certificate, including the details shown in the "Thermal Loads" table below.			
(d) The applicant must show on the plans accompanying the development application for the proposed development, all matters which the Thermal Comfort Protocol requires to be shown on those plans. Those plans must bear a stamp of endorsement from the Accredited Assessor, to certify that this is the case.	✔		
(e) The applicant must show on the plans accompanying the application for a construction certificate (or complying development certificate, if applicable), all thermal performance specifications set out in the Assessor Certificate, and all aspects of the proposed development which were used to calculate those specifications.		✔	
(f) The applicant must construct the development in accordance with all thermal performance specifications set out in the Assessor Certificate, and in accordance with those aspects of the development application or application for a complying development certificate which were used to calculate those specifications.		✔	✔
(g) Where there is an in-slab heating or cooling system, the applicant must:	✔	✔	✔

Notes

1. In these commitments, "applicant" means the person carrying out the development.
2. The applicant must identify each dwelling, building and common area listed in this certificate, on the plans accompanying any development application, and on the plans and specifications accompanying the application for a construction certificate / complying development certificate, for the proposed development, using the same identifying letter or reference as is given to that dwelling, building or common area in this certificate.
3. This note applies if the proposed development involves the erection of a building for both residential and non-residential purposes (or the change of use of a building for both residential and non-residential purposes). Commitments in this certificate which are specified to apply to a "common area" of a building or the development, apply only to that part of the building or development to be used for residential purposes.
4. If this certificate lists a central system as a commitment for a dwelling or building, and that system will also service any other dwelling or building within the development, then that system need only be installed once (even if it is separately listed as a commitment for that other dwelling or building).
5. If a star or other rating is specified in a commitment, this is a minimum rating.
6. All alternative water systems to be installed under these commitments (if any), must be installed in accordance with the requirements of all applicable regulatory authorities. NOTE: NSW Health does not recommend that stormwater, recycled water or private dam water be used to irrigate edible plants which are consumed raw, or that rainwater be used for human consumption in areas with potable water supply.

Legend

1. Commitments identified with a ✔ in the "Show on DA plans" column must be shown on the plans accompanying the development application for the proposed development (if a development application is to be lodged for the proposed development).
2. Commitments identified with a ✔ in the "Show on CC/CDC plans and specs" column must be shown in the plans and specifications accompanying the application for a construction certificate / complying development certificate for the proposed development.
3. Commitments identified with a ✔ in the "Certifier check" column must be certified by a certifying authority as having been fulfilled. (Note: a certifying authority must not issue an occupation certificate (either interim or final) for a building listed in this certificate, or for any part of such a building, unless it is satisfied that each of the commitments whose fulfilment it is required to monitor in relation to the building or part, has been fulfilled).

NOTES

- ALL WORKS TO BE IN ACCORDANCE WITH THE BUILDING CODE OF AUSTRALIA, AUSTRALIAN STANDARDS, STATUTORY REGULATIONS AND LOCAL AUTHORITY REQUIREMENTS.
- CONTRACTOR TO ENSURE CONSISTENCY BETWEEN SIMILAR MATERIAL IS MAINTAINED.
- PREPARE & MAKE GOOD ALL SURFACES & SUBSTRATE AS REQUIRED TO RECEIVE NEW FINISHES AS PER MANUFACTURER'S SPECIFICATION.
- ALL DIMENSIONS TO BE CHECKED ON SITE BEFORE COMMENCEMENT OF WORK. ALL DIMENSIONS MUST BE CHECKED & VERIFIED ON SITE PRIOR TO CONSTRUCTION & MANUFACTURE OF ANY ITEM.
- THIS DRAWING IS COPYRIGHT AND THE PROPERTY OF THE AUTHOR. IT MUST NOT BE RETAINED, COPIED OR USED WITHOUT THE EXPRESS AUTHORITY OF PLAY CO PTY LTD.

REV	DATE	DESCRIPTION
P1	19/09/25	PRELIMINARY PLAN
P2	08/12/25	PRELIMINARY PLAN
P3	21/01/26	PRELIMINARY PLAN
A	17/02/26	DA SUBMISSION
B	10/07/26	RFI
C	29/07/26	RFI

PROJECT
257 MARSDEN ROAD CARLINGFORD

ARCHITECT


PLAY CO ARCHITECTS
ARCHITECTURE | INTERIORS | PROJECT MANAGEMENT

PLAY CO PTY LTD

ABN 206 135 521 86
SUITE 801, 11 HELP STREET
CHATSWOOD NSW 2067
WWW.PLAY-CO.COM.AU
NOMINATED ARCHITECT
RAYMOND NG #8961
DESIGN PRACTITIONER DEP000234

CLIENT

PROJECT NUMBER	P632	PROJECT ADDRESS	257 MARSDEN ROAD CARLINGFORD
DRAWING NUMBER	A002	DRAWING TITLE	BASIX COMMITMENTS
SCALE		PAPER SIZE	A3
DRAWN BY	TT	REVIEWED BY	RN
REVISION	C	STATUS	RFI

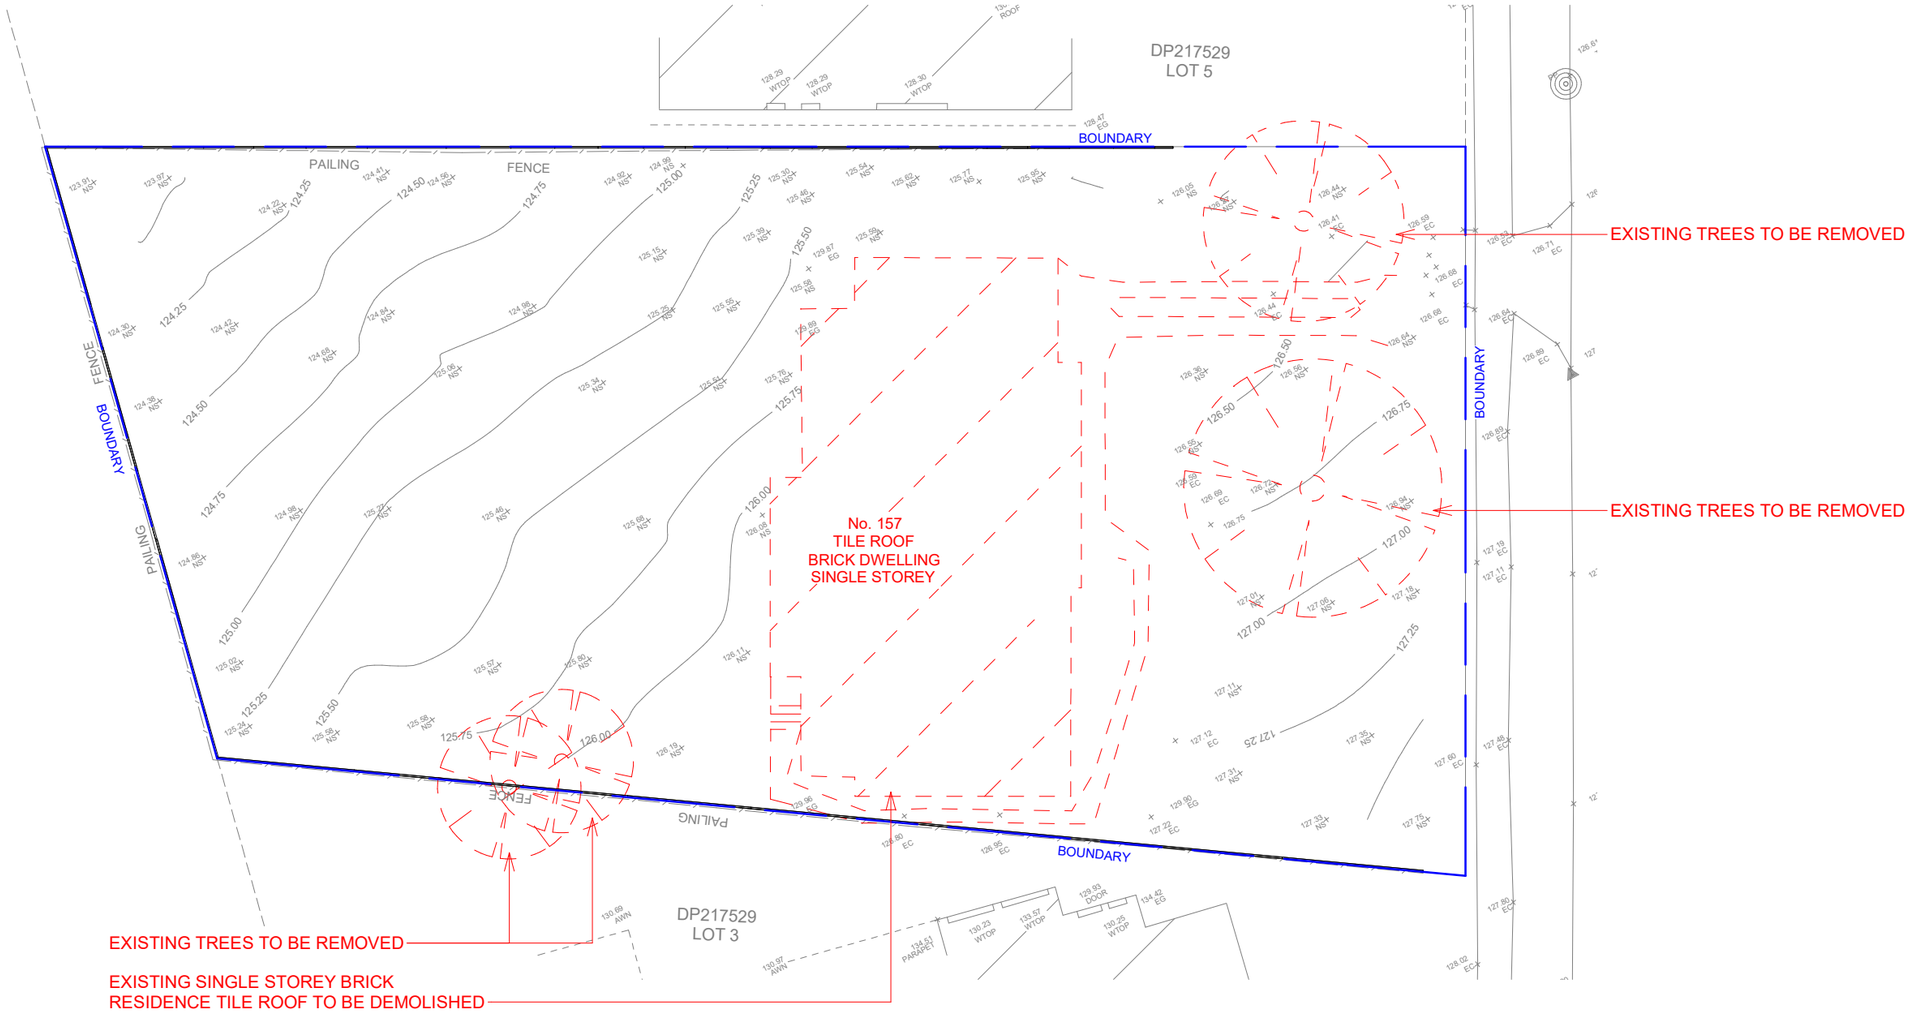

NOTES

- ALL WORKS TO BE IN ACCORDANCE WITH THE BUILDING CODE OF AUSTRALIA, AUSTRALIAN STANDARDS, STATUTORY REGULATIONS AND LOCAL AUTHORITY REQUIREMENTS.
- CONTRACTOR TO ENSURE CONSISTENCY BETWEEN SIMILAR MATERIAL IS MAINTAINED.
- PREPARE & MAKE GOOD ALL SURFACES & SUBSTRATE AS REQUIRED TO RECEIVE NEW FINISHES AS PER MANUFACTURER'S SPECIFICATION.
- ALL DIMENSIONS TO BE CHECKED ON SITE BEFORE COMMENCEMENT OF WORK. ALL DIMENSIONS MUST BE CHECKED & VERIFIED ON SITE PRIOR TO CONSTRUCTION & MANUFACTURE OF ANY ITEM.
- THIS DRAWING IS COPYRIGHT AND THE PROPERTY OF THE AUTHOR. IT MUST NOT BE RETAINED, COPIED OR USED WITHOUT THE EXPRESS AUTHORITY OF PLAY CO PTY LTD.

REV	DATE	DESCRIPTION
P1	19/09/25	PRELIMINARY PLAN
P2	08/12/25	PRELIMINARY PLAN
P3	21/01/26	PRELIMINARY PLAN
A	17/02/26	DA SUBMISSION
B	10/07/26	RFI
C	29/07/26	RFI


PROJECT
257 MARSDEN ROAD CARLINGFORD

ARCHITECT

PLAY CO ARCHITECTS
PLAY CO PTY LTD
ABN 206 135 521 86
SUITE 801, 11 HELP STREET
CHATSWOOD NSW 2067
WWW.PLAY-CO.COM.AU
NOMINATED ARCHITECT
RAYMOND NG #8961
DESIGN PRACTITIONER DEP000234

CLIENT

PROJECT NUMBER	P632	PROJECT ADDRESS	257 MARSDEN ROAD CARLINGFORD		
DRAWING NUMBER	A003	DRAWING TITLE	DEMOLITION PLAN		
SCALE	1 : 200	PAPER SIZE	A3	REVISION	C
DRAWN BY	TT	REVIEWED BY	RN	STATUS	RFI

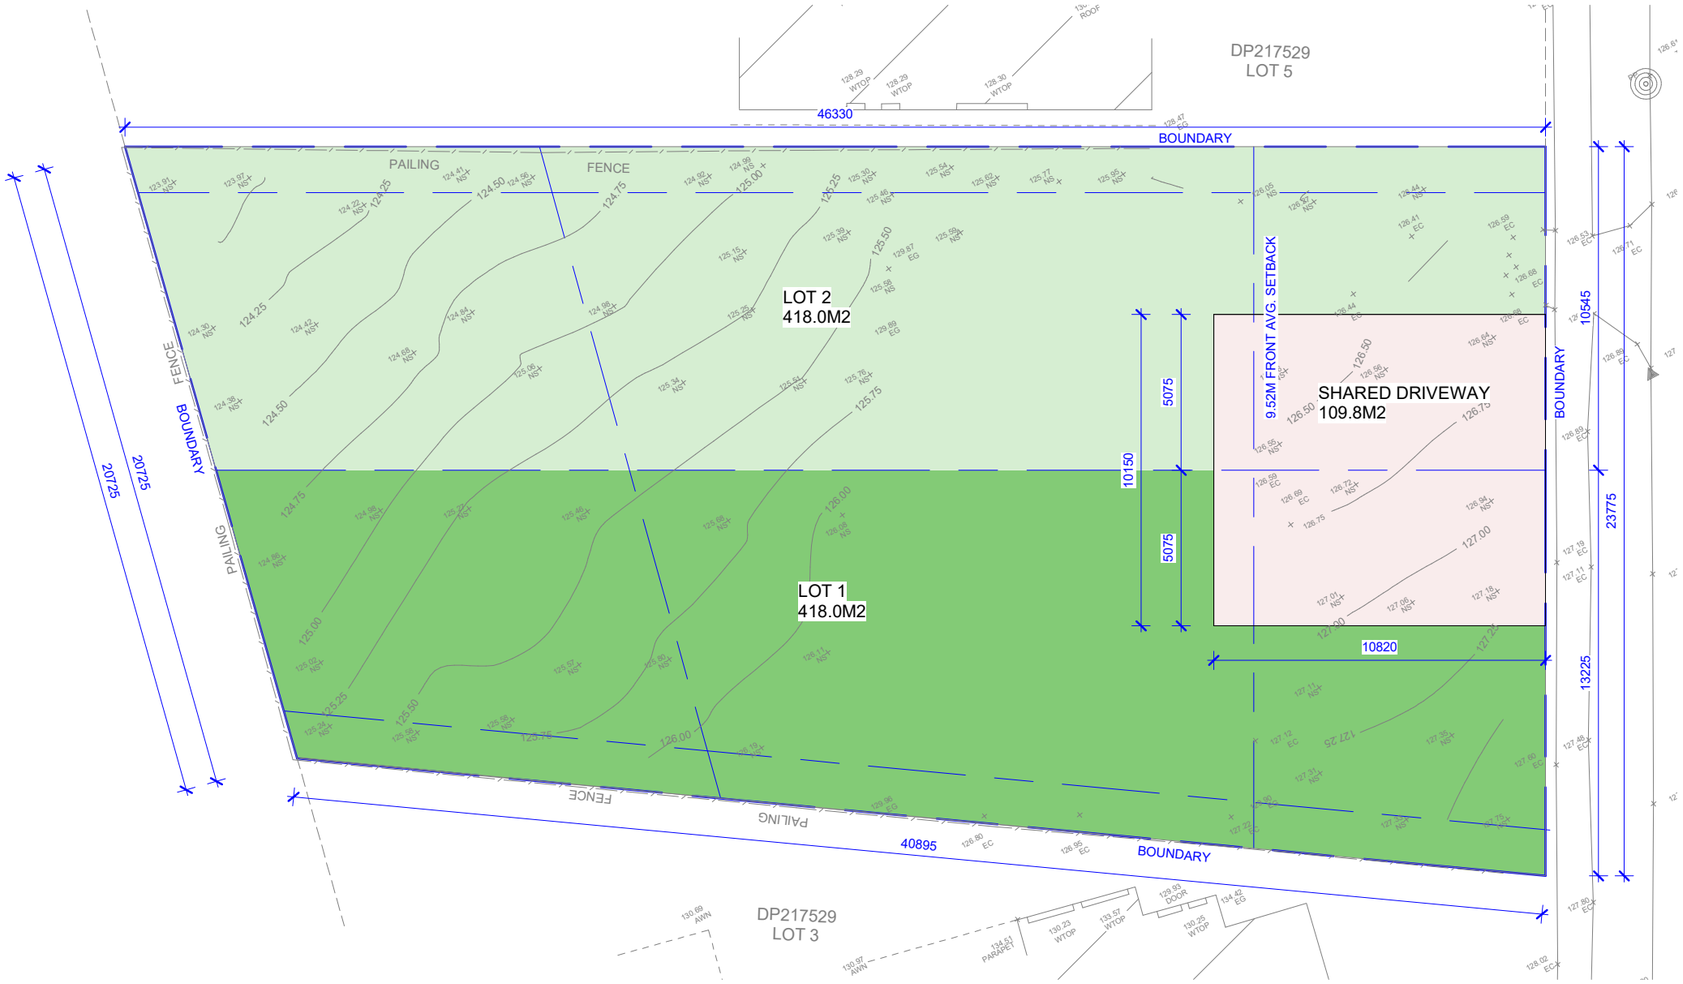

NOTES

- ALL WORKS TO BE IN ACCORDANCE WITH THE BUILDING CODE OF AUSTRALIA, AUSTRALIAN STANDARDS, STATUTORY REGULATIONS AND LOCAL AUTHORITY REQUIREMENTS.
- CONTRACTOR TO ENSURE CONSISTENCY BETWEEN SIMILAR MATERIAL IS MAINTAINED.
- PREPARE & MAKE GOOD ALL SURFACES & SUBSTRATE AS REQUIRED TO RECEIVE NEW FINISHES AS PER MANUFACTURER'S SPECIFICATION.
- ALL DIMENSIONS TO BE CHECKED ON SITE BEFORE COMMENCEMENT OF WORK. ALL DIMENSIONS MUST BE CHECKED & VERIFIED ON SITE PRIOR TO CONSTRUCTION & MANUFACTURE OF ANY ITEM.
- THIS DRAWING IS COPYRIGHT AND THE PROPERTY OF THE AUTHOR. IT MUST NOT BE RETAINED, COPIED OR USED WITHOUT THE EXPRESS AUTHORITY OF PLAY CO PTY LTD.

REV	DATE	DESCRIPTION
P1	19/09/25	PRELIMINARY PLAN
P2	08/12/25	PRELIMINARY PLAN
P3	21/01/26	PRELIMINARY PLAN
A	17/02/26	DA SUBMISSION
B	10/07/26	RFI
C	29/07/26	RFI

PROJECT
257 MARSDEN ROAD CARLINGFORD


ARCHITECT

PLAY CO PTY LTD

ABN 206 135 521 86
SUITE 801, 11 HELP STREET
CHATSWOOD NSW 2067
WWW.PLAY-CO.COM.AU
NOMINATED ARCHITECT
RAYMOND NG #8961
DESIGN PRACTITIONER DEP000234

CLIENT

PROJECT NUMBER	P632	PROJECT ADDRESS	257 MARSDEN ROAD CARLINGFORD
DRAWING NUMBER	A004	DRAWING TITLE	PROPOSED SUBDIVISION PLAN
SCALE	1 : 200	PAPER SIZE	A3
DRAWN BY	TT	REVIEWED BY	RN
REVISION	C	STATUS	RFI

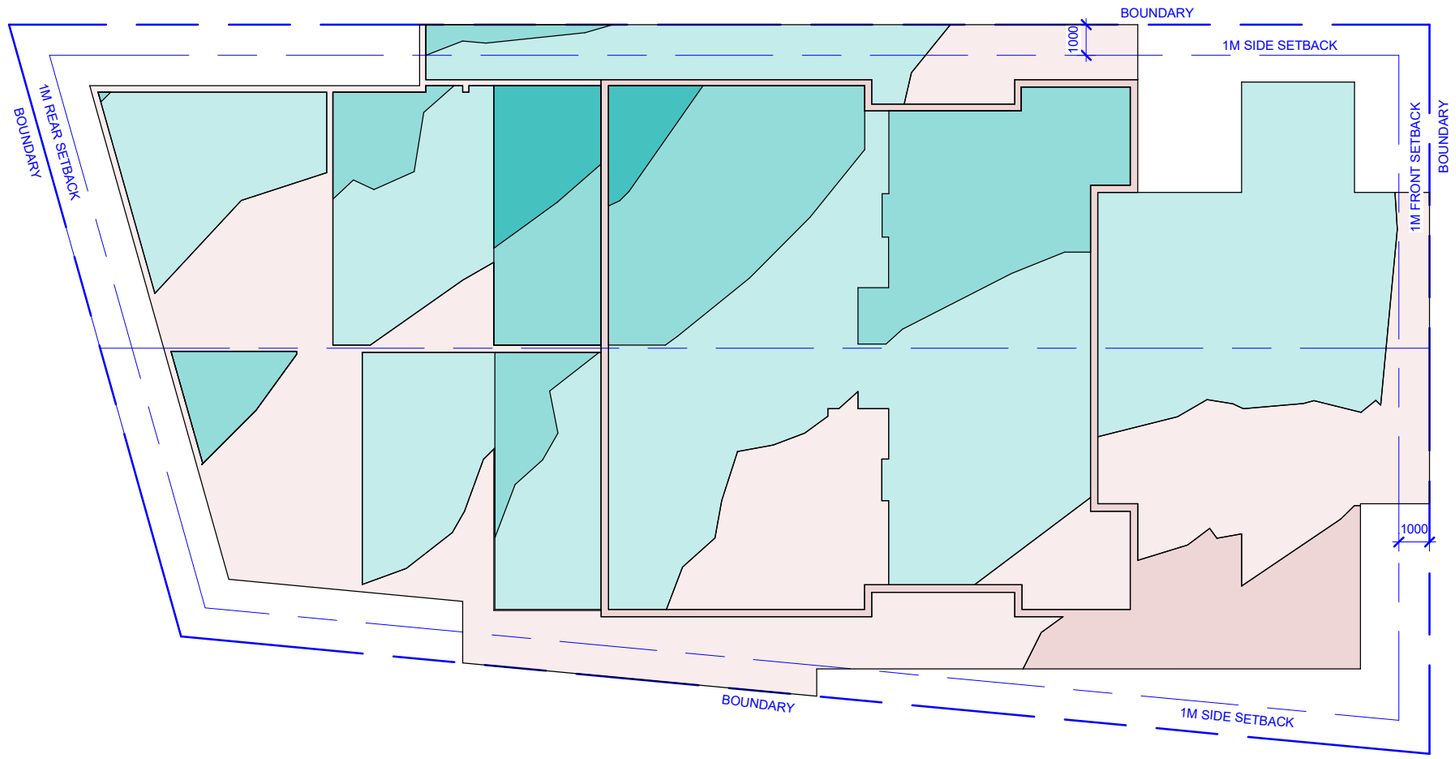

LEGEND

CUTTING AND FILLING DEPTH LANDSCAPE

CUT <1m	CUT <0.5m	FILL <0.5m	FILL <1m	FILL <1.25m

LANDSCAPE TO BE RETAINED

NOTES

- ALL WORKS TO BE IN ACCORDANCE WITH THE BUILDING CODE OF AUSTRALIA, AUSTRALIAN STANDARDS, STATUTORY REGULATIONS AND LOCAL AUTHORITY REQUIREMENTS.
- CONTRACTOR TO ENSURE CONSISTENCY BETWEEN SIMILAR MATERIAL IS MAINTAINED.
- PREPARE & MAKE GOOD ALL SURFACES & SUBSTRATE AS REQUIRED TO RECEIVE NEW FINISHES AS PER MANUFACTURER'S SPECIFICATION.
- ALL DIMENSIONS TO BE CHECKED ON SITE BEFORE COMMENCEMENT OF WORK. ALL DIMENSIONS MUST BE CHECKED & VERIFIED ON SITE PRIOR TO CONSTRUCTION & MANUFACTURE OF ANY ITEM.
- THIS DRAWING IS COPYRIGHT AND THE PROPERTY OF THE AUTHOR. IT MUST NOT BE RETAINED, COPIED OR USED WITHOUT THE EXPRESS AUTHORITY OF PLAY CO PTY LTD.

REV	DATE	DESCRIPTION
P1	19/09/25	PRELIMINARY PLAN
P2	08/12/25	PRELIMINARY PLAN
P3	21/01/26	PRELIMINARY PLAN
A	17/02/26	DA SUBMISSION
B	10/07/26	RFI
C	29/07/26	RFI

PROJECT

257 MARSDEN ROAD CARLINGFORD


ARCHITECT

PLAY CO ARCHITECTS
ARCHITECTURE | INTERIORS | PROJECT MANAGEMENT
PLAY CO PTY LTD
ABN 206 135 521 86
SUITE 801, 11 HELP STREET
CHATSWOOD NSW 2067
WWW.PLAY-CO.COM.AU
NOMINATED ARCHITECT
RAYMOND NG #8961
DESIGN PRACTITIONER DEP000234

CLIENT

PROJECT NUMBER	P632	PROJECT ADDRESS	257 MARSDEN ROAD CARLINGFORD
DRAWING NUMBER	A005	DRAWING TITLE	CUT AND FILL PLAN

SCALE	1 : 200	PAPER SIZE	A3	REVISION	C
DRAWN BY	TT	REVIEWED BY	RN	STATUS	RFI

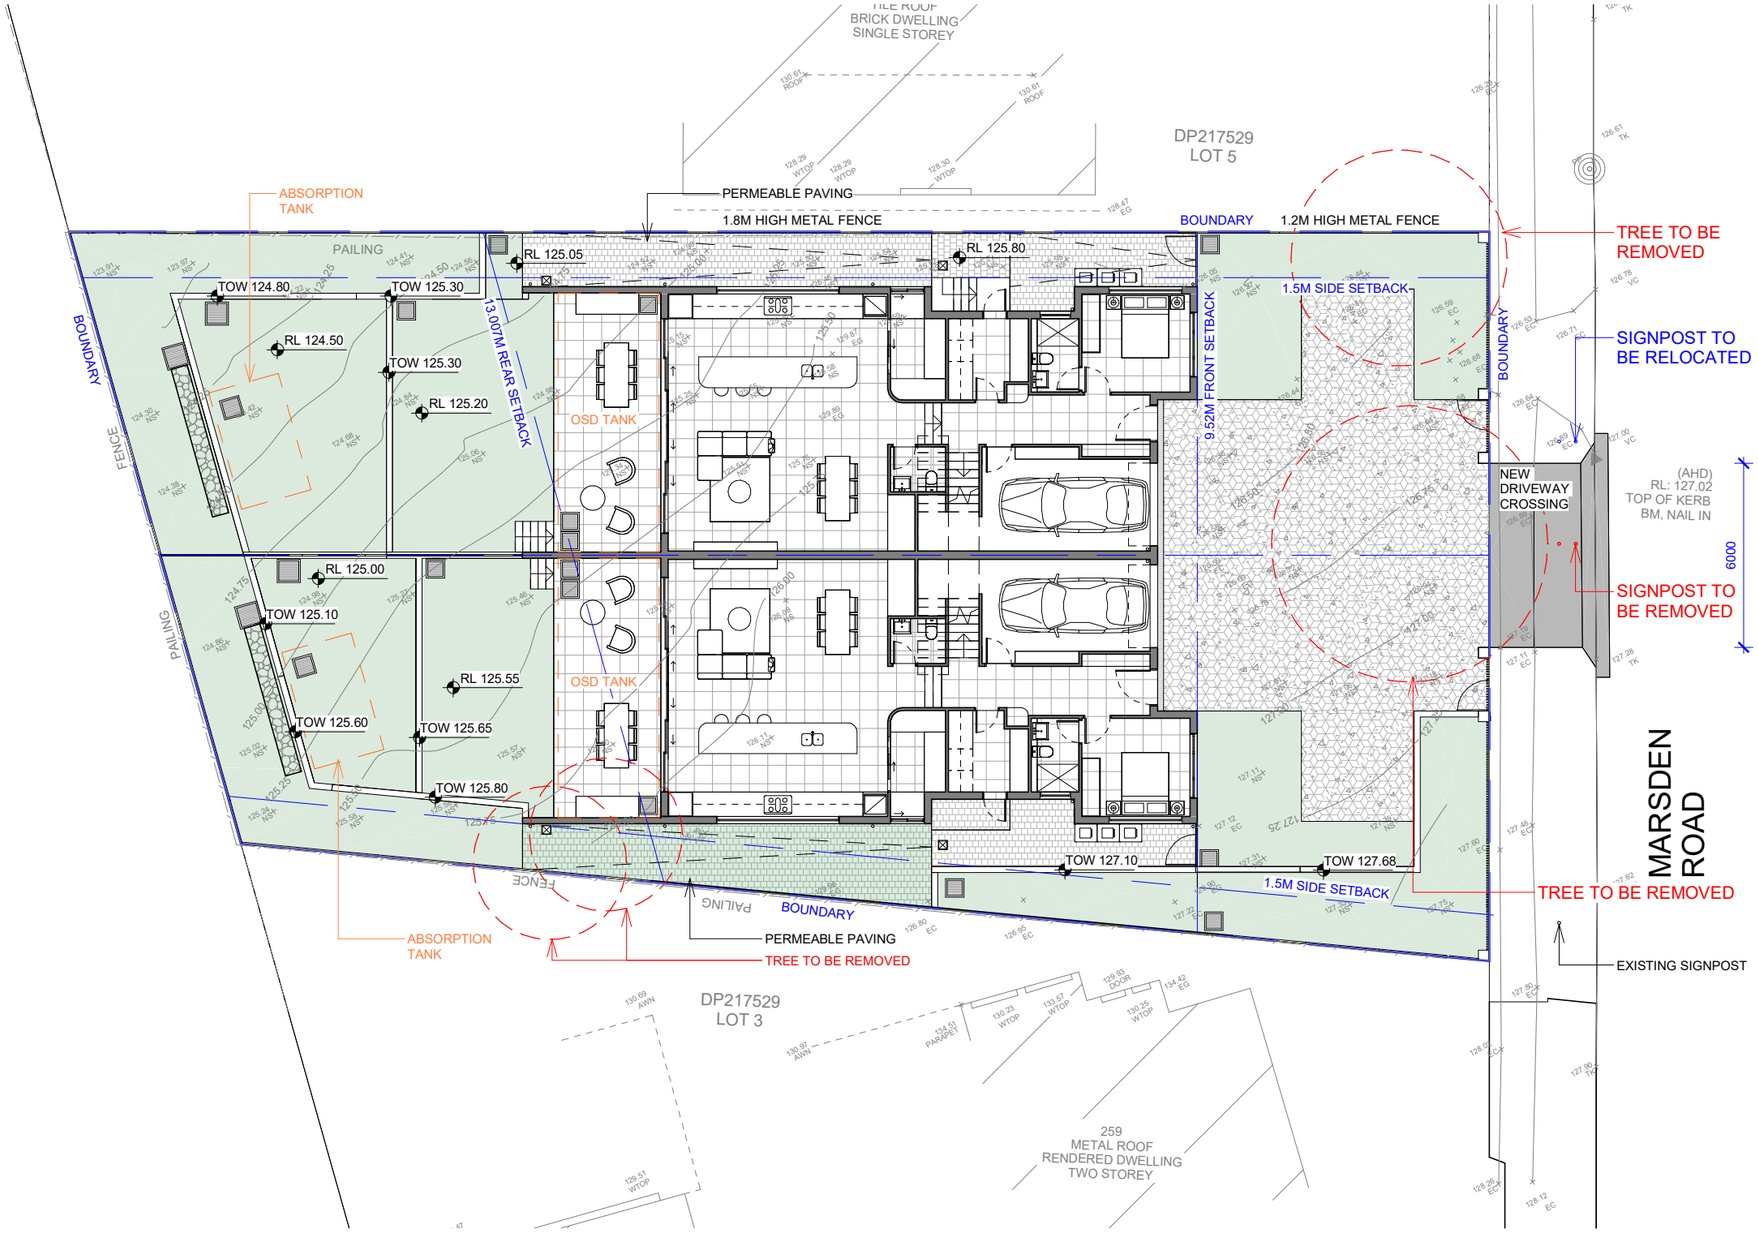

SITE DATA	
SITE AREA	942.20 m²
ZONING	R2
MAX GFA	471.10 m²

PROPOSED AREA - LOT 1 (No. 257)		PROPOSED AREA - LOT 2 (No. 257A)	
GROUND FLOOR	113.71 m²	GROUND FLOOR	113.71 m²
LEVEL 1	121.79 m²	LEVEL 1	121.79 m²
TOTAL	235.50 m²	TOTAL	235.50 m²
TOTAL PROPOSED AREA			471.00 m²

COMPLIANCE TABLE		
CONTROL	REQUIRED	PROPOSED
SITE AREA	400.00 m²	942.20 m²
PRIMARY RD SETBACK	9.52 m	9.52 m
SIDE SETBACK - GF	0.90 m	0.90 m
SIDE SETBACK - L1	1.90 m	1.90 m
REAR SETBACK - GF	3.00 m	3.00 m
REAR SETBACK - L1	8.00 m	8.00 m
MIN LANDSCAPED AREA	376.88 m²	341.47 m²
- FORWARD OF THE BUILDING LINE	0.00 m²	83.38 m²
- BEHIND OF THE BUILDING LINE	188.44 m²	258.09 m²
MIN DEEP SOIL	282.66 m²	209.59 m²
- FORWARD OF THE BUILDING LINE	56.53 m²	49.17 m²
- BEHIND OF THE BUILDING LINE	141.33 m²	160.42 m²
NUMBER OF PARKING	1	2

NOTES

- ALL WORKS TO BE IN ACCORDANCE WITH THE BUILDING CODE OF AUSTRALIA, AUSTRALIAN STANDARDS, STATUTORY REGULATIONS AND LOCAL AUTHORITY REQUIREMENTS.
- CONTRACTOR TO ENSURE CONSISTENCY BETWEEN SIMILAR MATERIAL IS MAINTAINED.
- PREPARE & MAKE GOOD ALL SURFACES & SUBSTRATE AS REQUIRED TO RECEIVE NEW FINISHES AS PER MANUFACTURER'S SPECIFICATION.
- ALL DIMENSIONS TO BE CHECKED ON SITE BEFORE COMMENCEMENT OF WORK. ALL DIMENSIONS MUST BE CHECKED & VERIFIED ON SITE PRIOR TO CONSTRUCTION & MANUFACTURE OF ANY ITEM.
- THIS DRAWING IS COPYRIGHT AND THE PROPERTY OF THE AUTHOR. IT MUST NOT BE RETAINED, COPIED OR USED WITHOUT THE EXPRESS AUTHORITY OF PLAY CO PTY LTD.

REV	DATE	DESCRIPTION
P1	19/09/25	PRELIMINARY PLAN
P2	08/12/25	PRELIMINARY PLAN
P3	21/01/26	PRELIMINARY PLAN
A	17/02/26	DA SUBMISSION
B	10/07/26	RFI
C	29/07/26	RFI


PROJECT
257 MARSDEN ROAD CARLINGFORD

ARCHITECT

PLAY CO ARCHITECTS
ARCHITECTURE | INTERIORS | PROJECT MANAGEMENT
PLAY CO PTY LTD
ABN 206 135 521 86
SUITE 801, 11 HELP STREET
CHATSWOOD NSW 2067
WWW.PLAY-CO.COM.AU
NOMINATED ARCHITECT
RAYMOND NG #8961
DESIGN PRACTITIONER DEP000234

CLIENT

PROJECT NUMBER	P632	PROJECT ADDRESS	257 MARSDEN ROAD CARLINGFORD
DRAWING NUMBER	A100	DRAWING TITLE	PROPOSED SITE PLAN
SCALE	1 : 200	PAPER SIZE	A3
REVISION	C		
DRAWN BY	TT	REVIEWED BY	RN
STATUS	RFI		

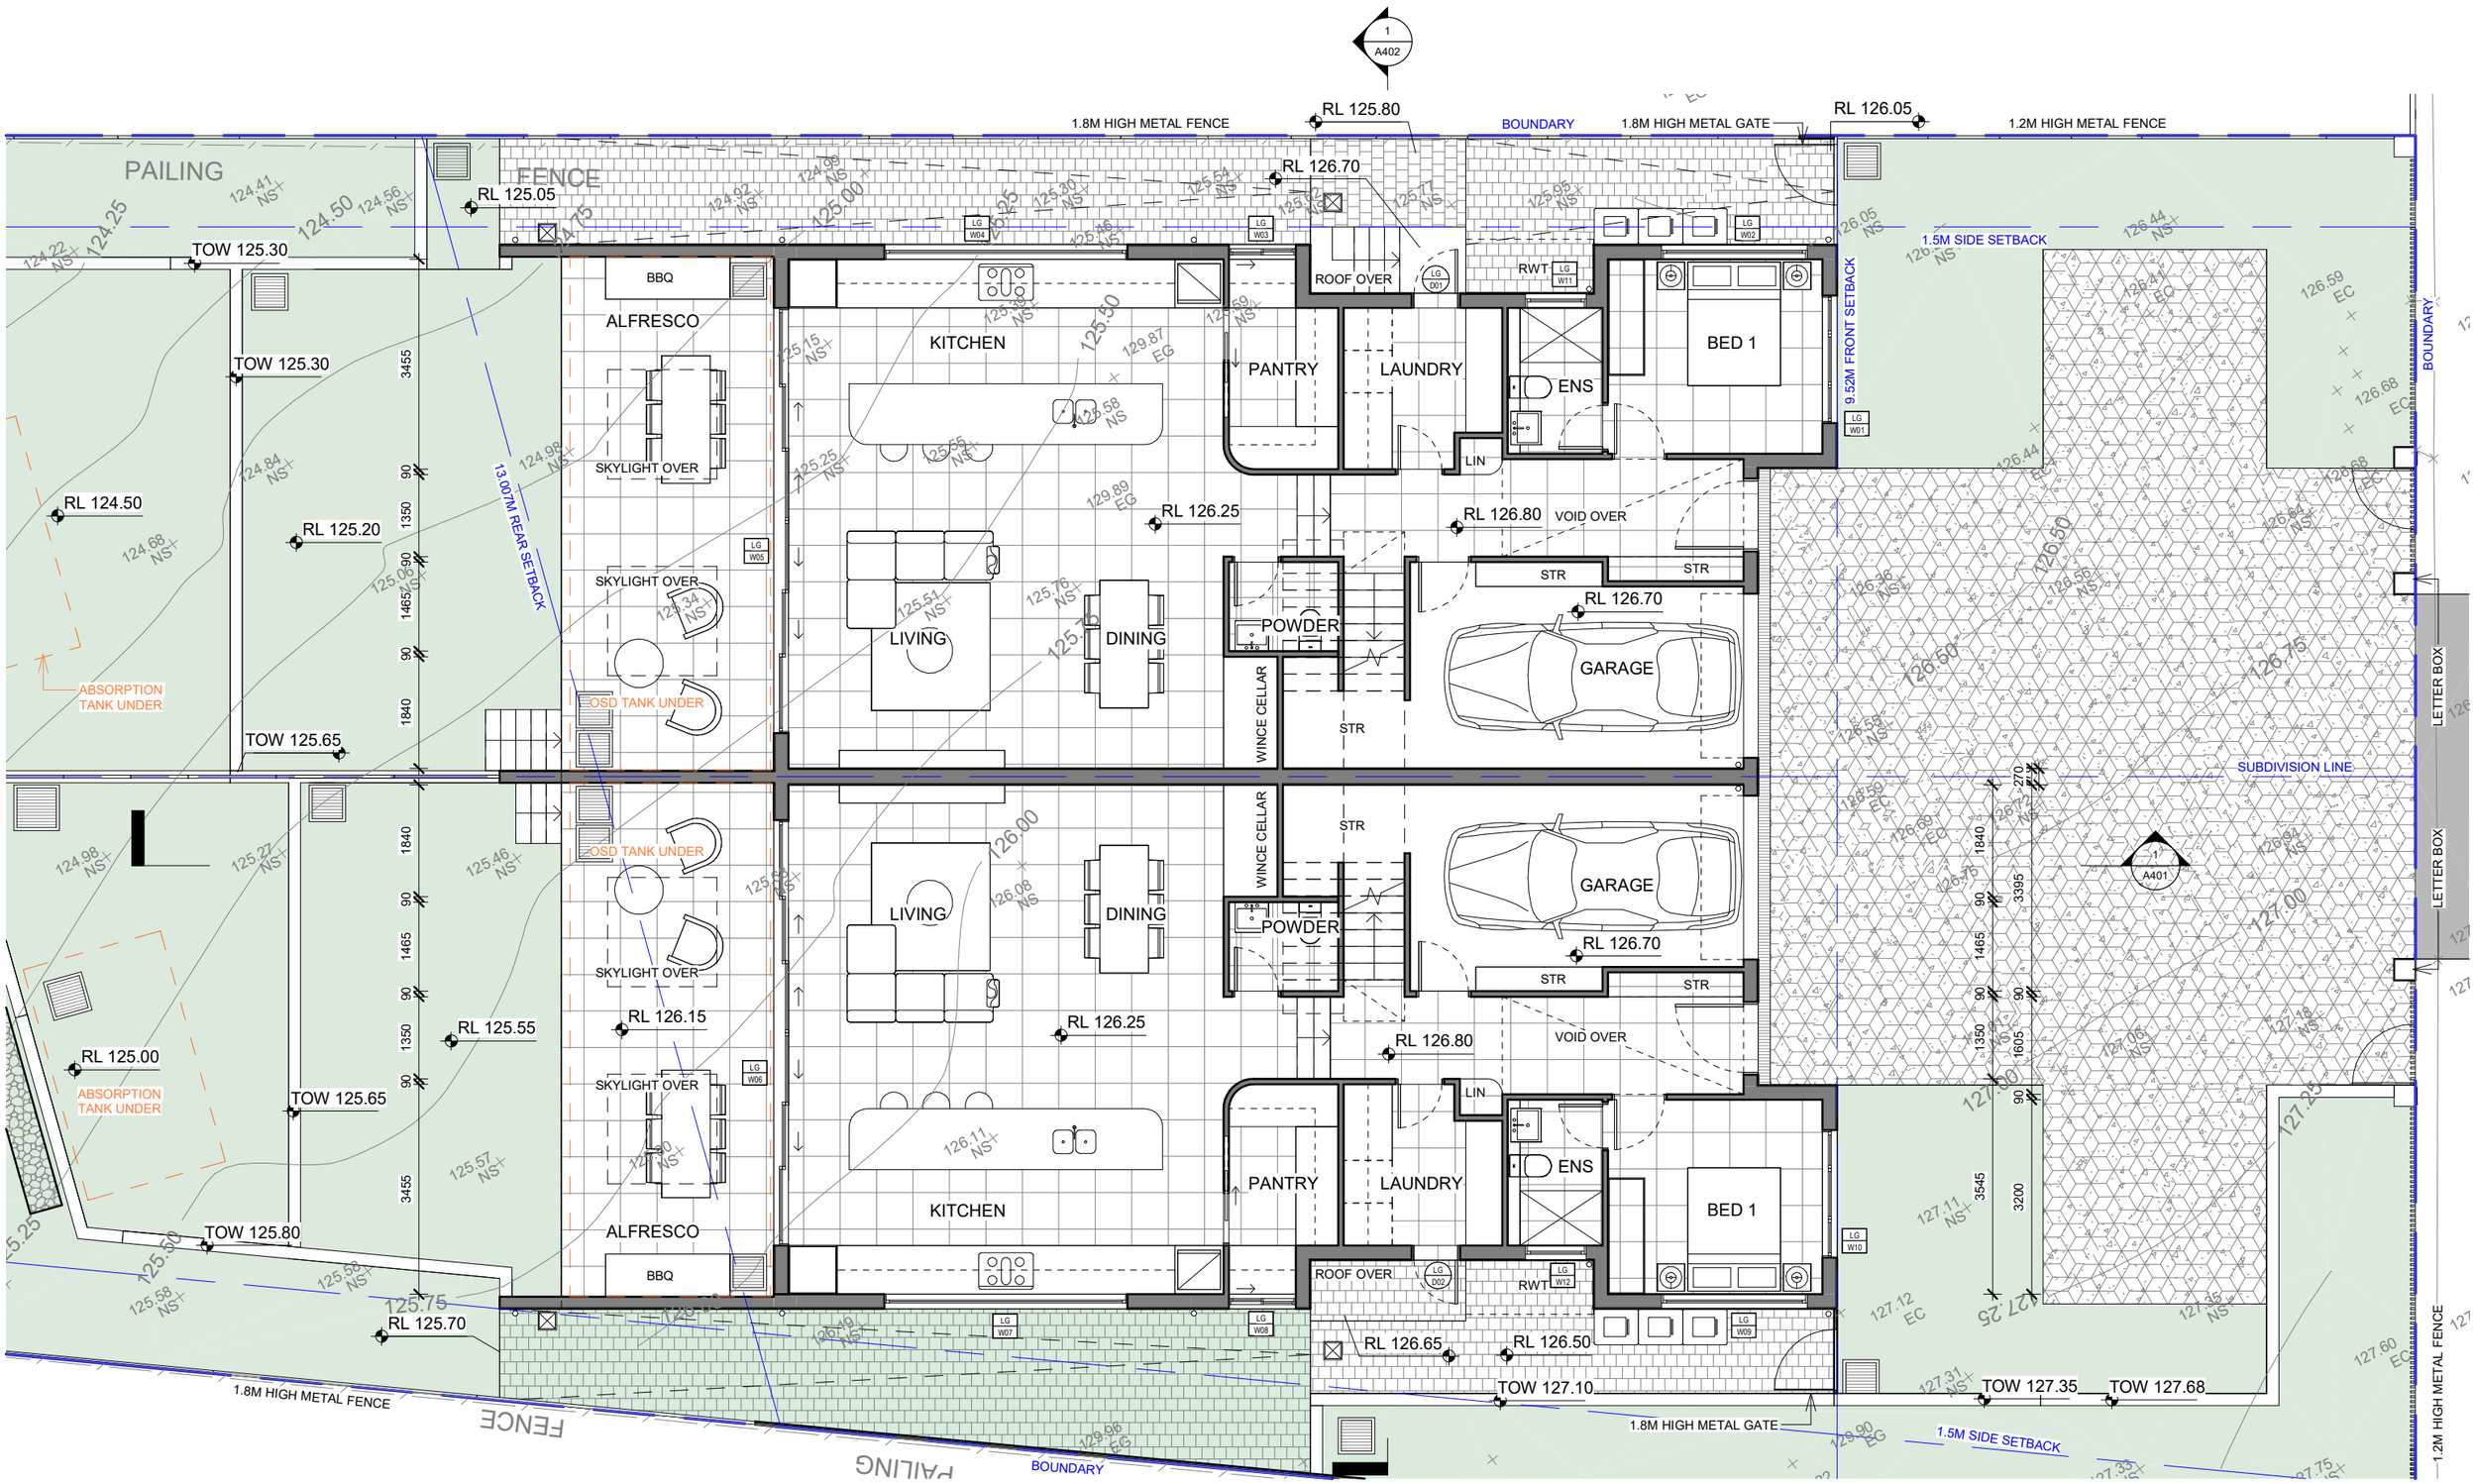

NOTES

- ALL WORKS TO BE IN ACCORDANCE WITH THE BUILDING CODE OF AUSTRALIA, AUSTRALIAN STANDARDS, STATUTORY REGULATIONS AND LOCAL AUTHORITY REQUIREMENTS.
- CONTRACTOR TO ENSURE CONSISTENCY BETWEEN SIMILAR MATERIAL IS MAINTAINED.
- PREPARE & MAKE GOOD ALL SURFACES & SUBSTRATE AS REQUIRED TO RECEIVE NEW FINISHES AS PER MANUFACTURER'S SPECIFICATION.
- ALL DIMENSIONS TO BE CHECKED ON SITE BEFORE COMMENCEMENT OF WORK. ALL DIMENSIONS MUST BE CHECKED & VERIFIED ON SITE PRIOR TO CONSTRUCTION & MANUFACTURE OF ANY ITEM.
- THIS DRAWING IS COPYRIGHT AND THE PROPERTY OF THE AUTHOR. IT MUST NOT BE RETAINED, COPIED OR USED WITHOUT THE EXPRESS AUTHORITY OF PLAY CO PTY LTD.

REV	DATE	DESCRIPTION
P1	19/09/25	PRELIMINARY PLAN
P2	08/12/25	PRELIMINARY PLAN
P3	21/01/26	PRELIMINARY PLAN
A	17/02/26	DA SUBMISSION
B	10/07/26	RFI
C	29/07/26	RFI


PROJECT
257 MARSDEN ROAD CARLINGFORD

ARCHITECT

PLAY CO ARCHITECTS
PLAY CO PTY LTD
ABN 206 135 521 86
SUITE 801, 11 HELP STREET
CHATSWOOD NSW 2067
WWW.PLAY-CO.COM.AU
NOMINATED ARCHITECT
RAYMOND NG #8961
DESIGN PRACTITIONER DEP000234

CLIENT

PROJECT NUMBER	P632	PROJECT ADDRESS	257 MARSDEN ROAD CARLINGFORD
DRAWING NUMBER	A201	DRAWING TITLE	PROPOSED GROUND FLOOR PLAN
SCALE	1 : 100	PAPER SIZE	A3
REVISION	C		
DRAWN BY	TT	REVIEWED BY	RN
STATUS	RFI		

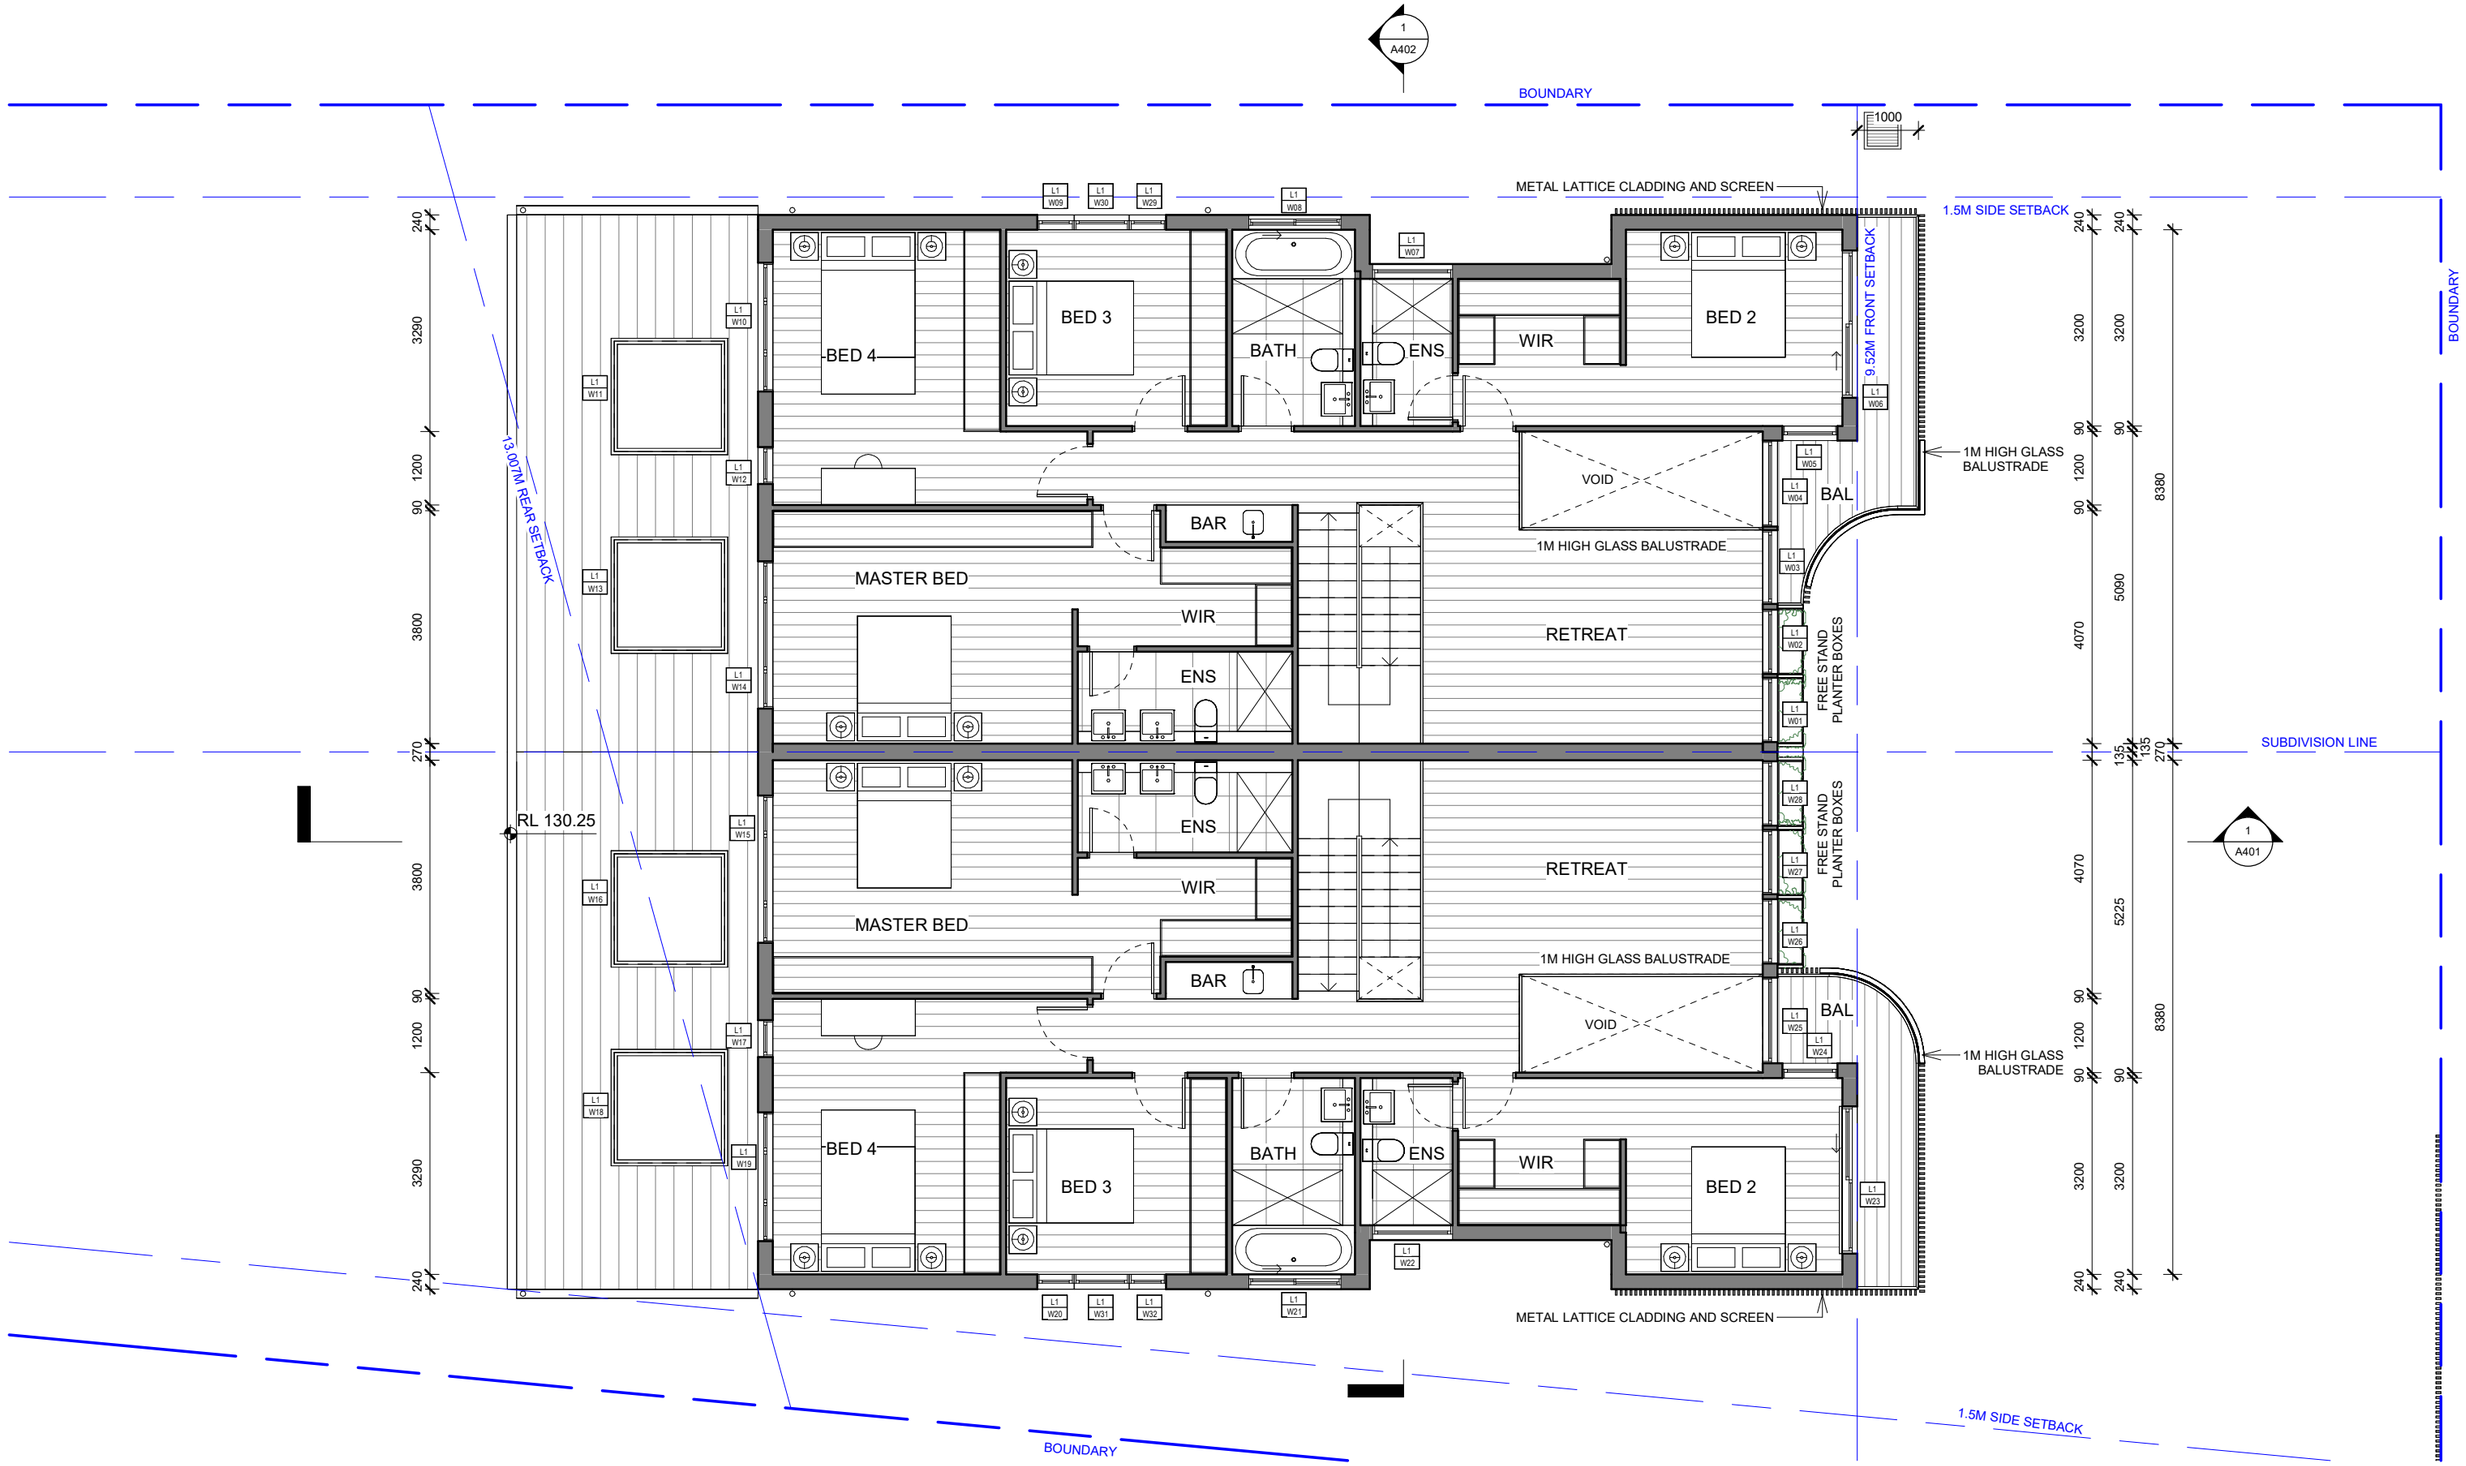

NOTES

- ALL WORKS TO BE IN ACCORDANCE WITH THE BUILDING CODE OF AUSTRALIA, AUSTRALIAN STANDARDS, STATUTORY REGULATIONS AND LOCAL AUTHORITY REQUIREMENTS.
- CONTRACTOR TO ENSURE CONSISTENCY BETWEEN SIMILAR MATERIAL IS MAINTAINED.
- PREPARE & MAKE GOOD ALL SURFACES & SUBSTRATE AS REQUIRED TO RECEIVE NEW FINISHES AS PER MANUFACTURER'S SPECIFICATION.
- ALL DIMENSIONS TO BE CHECKED ON SITE BEFORE COMMENCEMENT OF WORK. ALL DIMENSIONS MUST BE CHECKED & VERIFIED ON SITE PRIOR TO CONSTRUCTION & MANUFACTURE OF ANY ITEM.
- THIS DRAWING IS COPYRIGHT AND THE PROPERTY OF THE AUTHOR. IT MUST NOT BE RETAINED, COPIED OR USED WITHOUT THE EXPRESS AUTHORITY OF PLAY CO PTY LTD.

REV	DATE	DESCRIPTION
P1	19/09/25	PRELIMINARY PLAN
P2	08/12/25	PRELIMINARY PLAN
P3	21/01/26	PRELIMINARY PLAN
A	17/02/26	DA SUBMISSION
B	10/07/26	RFI
C	29/07/26	RFI

PROJECT


257 MARSDEN ROAD CARLINGFORD

ARCHITECT

PLAY CO ARCHITECTS
PLAY CO PTY LTD
ABN 206 135 521 86
SUITE 801, 11 HELP STREET
CHATSWOOD NSW 2067
WWW.PLAY-CO.COM.AU
NOMINATED ARCHITECT
RAYMOND NG #8961
DESIGN PRACTITIONER DEP000234

CLIENT

PROJECT NUMBER	P632	PROJECT ADDRESS	257 MARSDEN ROAD CARLINGFORD
DRAWING NUMBER	A205	DRAWING TITLE	PROPOSED FIRST FLOOR PLAN
SCALE	1 : 100	PAPER SIZE	A3
REVISION	C		
DRAWN BY	TT	REVIEWED BY	RN
STATUS	RFI		

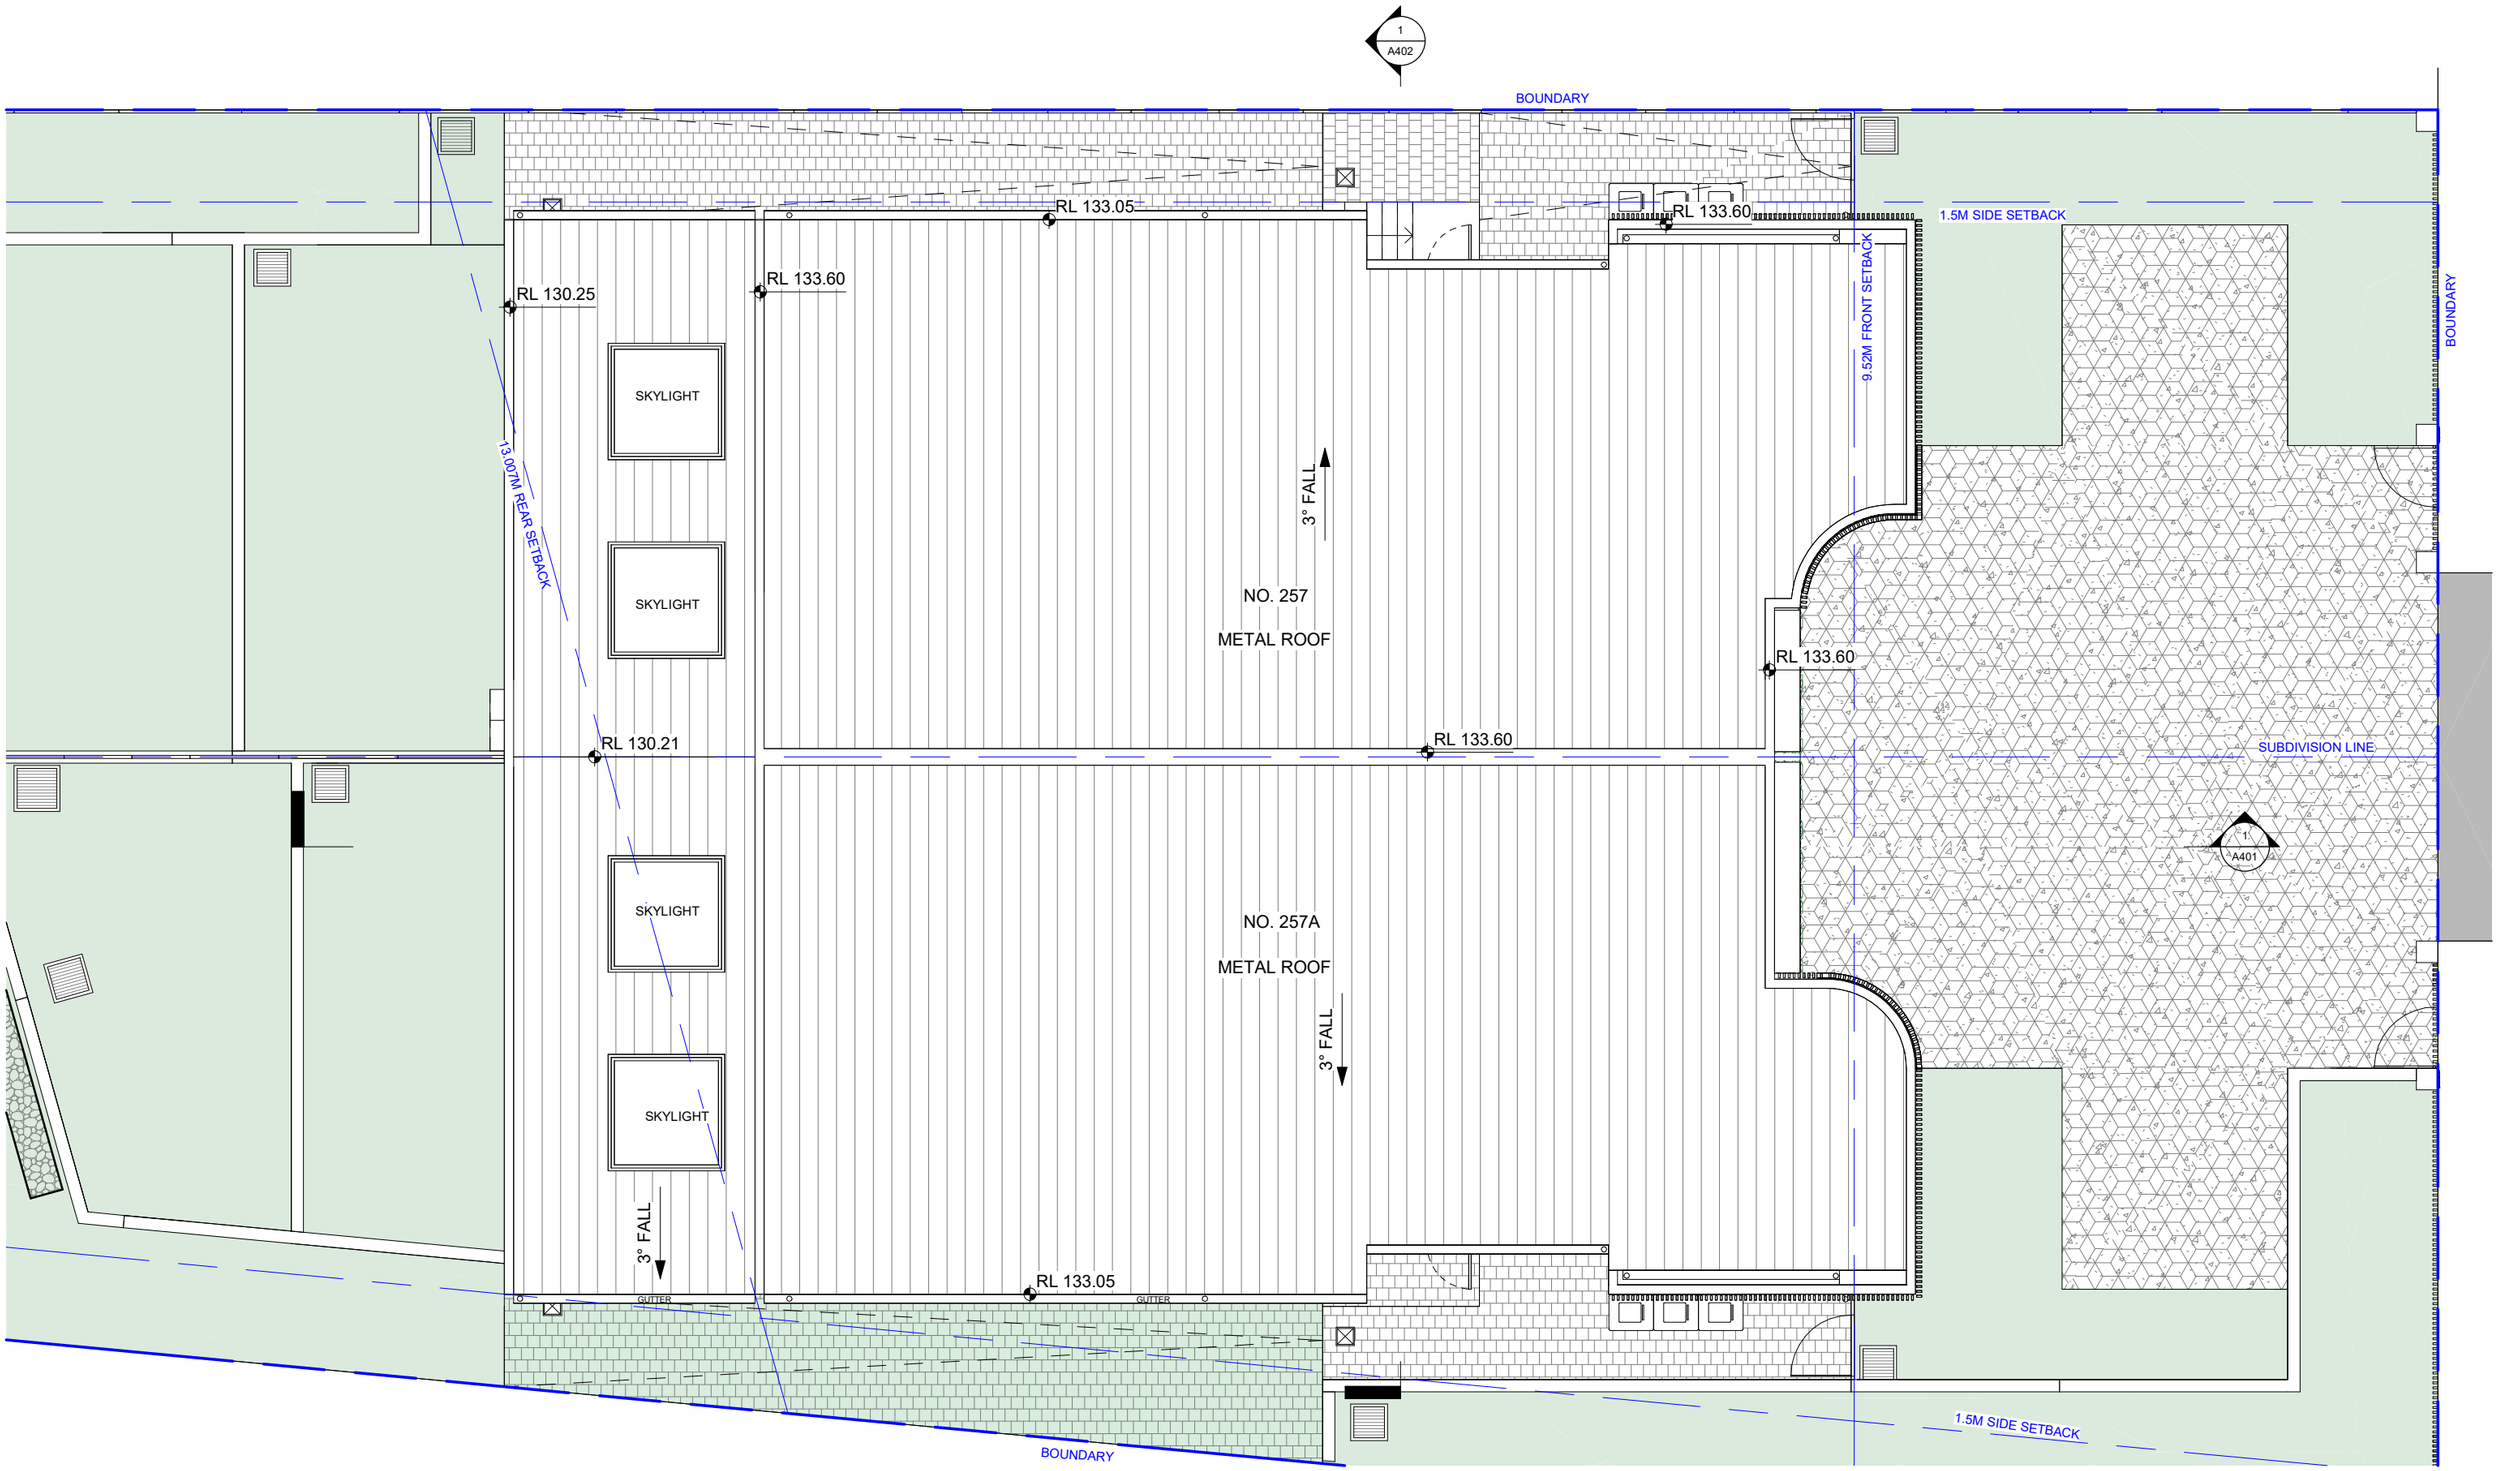

NOTES

- ALL WORKS TO BE IN ACCORDANCE WITH THE BUILDING CODE OF AUSTRALIA, AUSTRALIAN STANDARDS, STATUTORY REGULATIONS AND LOCAL AUTHORITY REQUIREMENTS.
- CONTRACTOR TO ENSURE CONSISTENCY BETWEEN SIMILAR MATERIAL IS MAINTAINED.
- PREPARE & MAKE GOOD ALL SURFACES & SUBSTRATE AS REQUIRED TO RECEIVE NEW FINISHES AS PER MANUFACTURER'S SPECIFICATION.
- ALL DIMENSIONS TO BE CHECKED ON SITE BEFORE COMMENCEMENT OF WORK. ALL DIMENSIONS MUST BE CHECKED & VERIFIED ON SITE PRIOR TO CONSTRUCTION & MANUFACTURE OF ANY ITEM.
- THIS DRAWING IS COPYRIGHT AND THE PROPERTY OF THE AUTHOR. IT MUST NOT BE RETAINED, COPIED OR USED WITHOUT THE EXPRESS AUTHORITY OF PLAY CO PTY LTD.

REV	DATE	DESCRIPTION
P1	19/09/25	PRELIMINARY PLAN
P2	08/12/25	PRELIMINARY PLAN
P3	21/01/26	PRELIMINARY PLAN
A	17/02/26	DA SUBMISSION
B	10/07/26	RFI
C	29/07/26	RFI

PROJECT

257 MARSDEN ROAD CARLINGFORD

ARCHITECT

PLAY CO ARCHITECTS
ARCHITECTURE | INTERIORS | PROJECT MANAGEMENT
PLAY CO PTY LTD
ABN 206 135 521 86
SUITE 801, 11 HELP STREET
CHATSWOOD NSW 2067
WWW.PLAY-CO.COM.AU
NOMINATED ARCHITECT
RAYMOND NG #8961
DESIGN PRACTITIONER DEP000234

CLIENT

PROJECT NUMBER	P632	PROJECT ADDRESS	257 MARSDEN ROAD CARLINGFORD
DRAWING NUMBER	A206	DRAWING TITLE	PROPOSED ROOF PLAN
SCALE	1 : 100	PAPER SIZE	A3
REVISION	C		
DRAWN BY	TT	REVIEWED BY	RN
STATUS	RFI		



MF1 WHITE POWDERCOATED ALUMINIUM METAL LOUVERS



MF2 WHITE POWDERCOATED ALUMINIUM VERTICAL METAL LATTICE TO FRONT FENCE



PT1 VIVID WHITE DULUX EXTERIOR RENDER AND PAINT FINISH



PT2 MONUTEMENT DULUX EXTERIOR RENDER AND PAINT FINISH



AL1 MONUMENT POWDERCOATED ALUMINIUM FRAME TO WINDOWS AND DOORS

PC1

PC2 WHITE POWDER COATED ALUMINIUM



GD MONUMENT GARAGE DOOR



MR1 WINDSPRAY COLORBOND METAL ROOF

NOTES

- ALL WORKS TO BE IN ACCORDANCE WITH THE BUILDING CODE OF AUSTRALIA, AUSTRALIAN STANDARDS, STATUTORY REGULATIONS AND LOCAL AUTHORITY REQUIREMENTS.
- CONTRACTOR TO ENSURE CONSISTENCY BETWEEN SIMILAR MATERIAL IS MAINTAINED.
- PREPARE & MAKE GOOD ALL SURFACES & SUBSTRATE AS REQUIRED TO RECEIVE NEW FINISHES AS PER MANUFACTURER'S SPECIFICATION.
- ALL DIMENSIONS TO BE CHECKED ON SITE BEFORE COMMENCEMENT OF WORK. ALL DIMENSIONS MUST BE CHECKED & VERIFIED ON SITE PRIOR TO CONSTRUCTION & MANUFACTURE OF ANY ITEM.
- THIS DRAWING IS COPYRIGHT AND THE PROPERTY OF THE AUTHOR. IT MUST NOT BE RETAINED, COPIED OR USED WITHOUT THE EXPRESS AUTHORITY OF PLAY CO PTY LTD.

REV	DATE	DESCRIPTION
P1	19/09/25	PRELIMINARY PLAN
P2	08/12/25	PRELIMINARY PLAN
P3	21/01/26	PRELIMINARY PLAN
A	17/02/26	DA SUBMISSION
B	10/07/26	RFI
C	29/07/26	RFI

PROJECT
257 MARSDEN ROAD CARLINGFORD

ARCHITECT

PLAY CO ARCHITECTS
PLAY CO PTY LTD
ABN 206 135 521 86
SUITE 801, 11 HELP STREET
CHATSWOOD NSW 2067
WWW.PLAY-CO.COM.AU
NOMINATED ARCHITECT
RAYMOND NG #8961
DESIGN PRACTITIONER DEP000234

CLIENT

PROJECT NUMBER	P632	PROJECT ADDRESS	257 MARSDEN ROAD CARLINGFORD		
DRAWING NUMBER	A300	DRAWING TITLE	FINISHED MATERIAL BOARD		
SCALE		PAPER SIZE	A3	REVISION	C
DRAWN BY	TT	REVIEWED BY	RN	STATUS	RFI



NOTES

- ALL WORKS TO BE IN ACCORDANCE WITH THE BUILDING CODE OF AUSTRALIA, AUSTRALIAN STANDARDS, STATUTORY REGULATIONS AND LOCAL AUTHORITY REQUIREMENTS.
- CONTRACTOR TO ENSURE CONSISTENCY BETWEEN SIMILAR MATERIAL IS MAINTAINED.
- PREPARE & MAKE GOOD ALL SURFACES & SUBSTRATE AS REQUIRED TO RECEIVE NEW FINISHES AS PER MANUFACTURER'S SPECIFICATION.
- ALL DIMENSIONS TO BE CHECKED ON SITE BEFORE COMMENCEMENT OF WORK. ALL DIMENSIONS MUST BE CHECKED & VERIFIED ON SITE PRIOR TO CONSTRUCTION & MANUFACTURE OF ANY ITEM.
- THIS DRAWING IS COPYRIGHT AND THE PROPERTY OF THE AUTHOR. IT MUST NOT BE RETAINED, COPIED OR USED WITHOUT THE EXPRESS AUTHORITY OF PLAY CO PTY LTD.

REV	DATE	DESCRIPTION
P1	19/09/25	PRELIMINARY PLAN
P2	08/12/25	PRELIMINARY PLAN
P3	21/01/26	PRELIMINARY PLAN
A	17/02/26	DA SUBMISSION
B	10/07/26	RFI
C	29/07/26	RFI

PROJECT

257 MARSDEN ROAD CARLINGFORD


ARCHITECT

PLAY CO PTY LTD

ABN 206 135 521 86
SUITE 801, 11 HELP STREET
CHATSWOOD NSW 2067
WWW.PLAY-CO.COM.AU
NOMINATED ARCHITECT
RAYMOND NG #8961
DESIGN PRACTITIONER DEP000234

CLIENT

PROJECT NUMBER	P632	PROJECT ADDRESS	257 MARSDEN ROAD CARLINGFORD
DRAWING NUMBER	A301	DRAWING TITLE	SOUTH ELEVATION
SCALE	1 : 100	PAPER SIZE	A3
DRAWN BY	TT	REVIEWED BY	RN
REVISION	C	STATUS	RFI

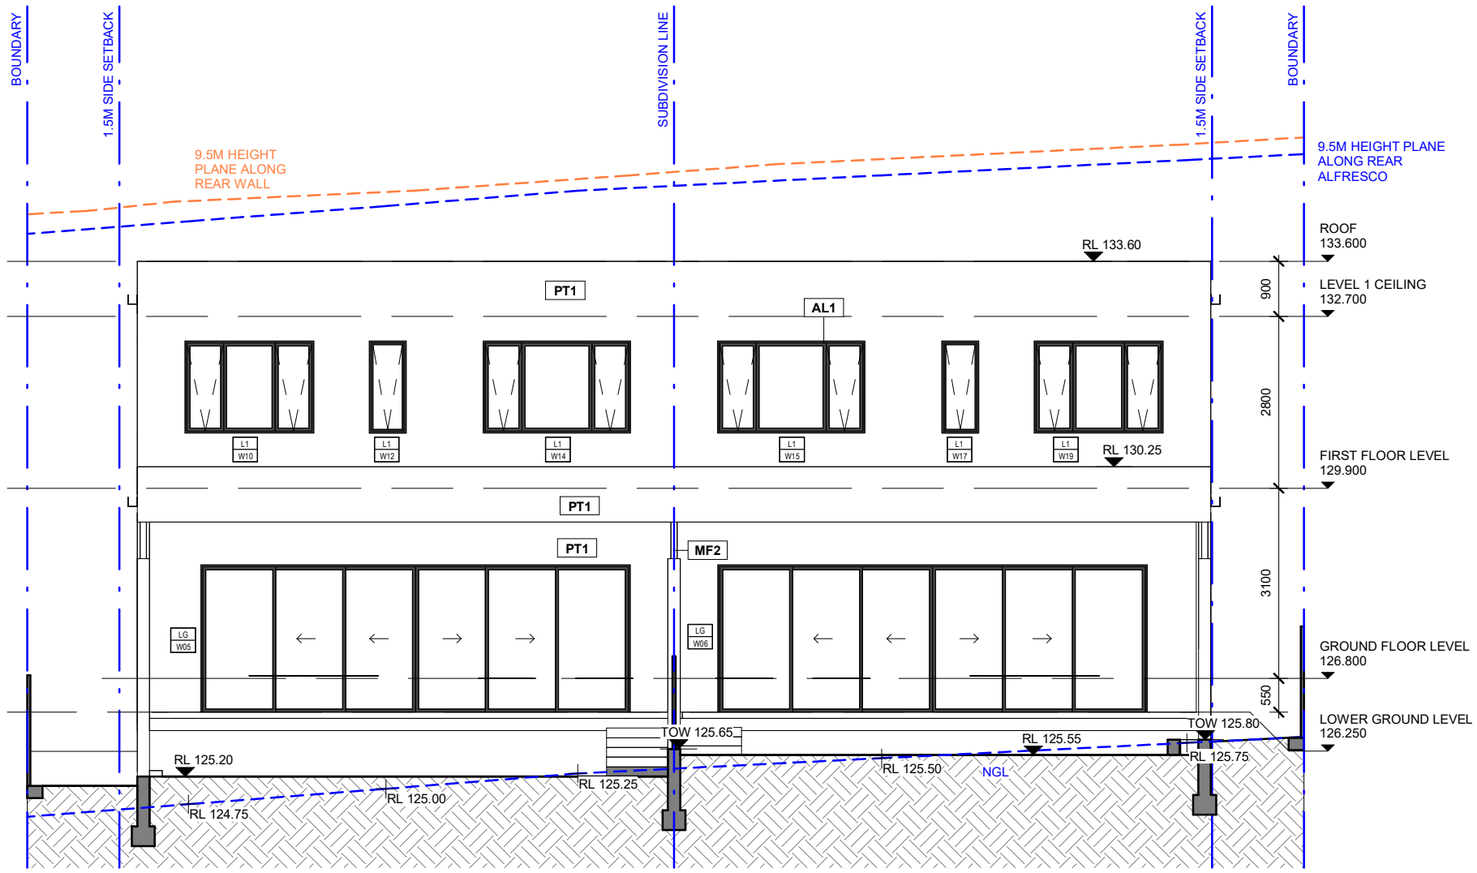

NOTES

- ALL WORKS TO BE IN ACCORDANCE WITH THE BUILDING CODE OF AUSTRALIA, AUSTRALIAN STANDARDS, STATUTORY REGULATIONS AND LOCAL AUTHORITY REQUIREMENTS.
- CONTRACTOR TO ENSURE CONSISTENCY BETWEEN SIMILAR MATERIAL IS MAINTAINED.
- PREPARE & MAKE GOOD ALL SURFACES & SUBSTRATE AS REQUIRED TO RECEIVE NEW FINISHES AS PER MANUFACTURER'S SPECIFICATION.
- ALL DIMENSIONS TO BE CHECKED ON SITE BEFORE COMMENCEMENT OF WORK. ALL DIMENSIONS MUST BE CHECKED & VERIFIED ON SITE PRIOR TO CONSTRUCTION & MANUFACTURE OF ANY ITEM.
- THIS DRAWING IS COPYRIGHT AND THE PROPERTY OF THE AUTHOR. IT MUST NOT BE RETAINED, COPIED OR USED WITHOUT THE EXPRESS AUTHORITY OF PLAY CO PTY LTD.

REV	DATE	DESCRIPTION
P1	19/09/25	PRELIMINARY PLAN
P2	08/12/25	PRELIMINARY PLAN
P3	21/01/26	PRELIMINARY PLAN
A	17/02/26	DA SUBMISSION
B	10/07/26	RFI
C	29/07/26	RFI

PROJECT


257 MARSDEN ROAD CARLINGFORD

ARCHITECT

PLAY CO ARCHITECTS
PLAY CO PTY LTD
ABN 206 135 521 86
SUITE 801, 11 HELP STREET
CHATSWOOD NSW 2067
WWW.PLAY-CO.COM.AU
NOMINATED ARCHITECT
RAYMOND NG #8961
DESIGN PRACTITIONER DEP000234

CLIENT

PROJECT NUMBER	P632	PROJECT ADDRESS	257 MARSDEN ROAD CARLINGFORD
DRAWING NUMBER	A302	DRAWING TITLE	NORTH ELEVATION
SCALE	1 : 100	PAPER SIZE	A3
DRAWN BY	TT	REVIEWED BY	RN
		REVISION	C
		STATUS	RFI

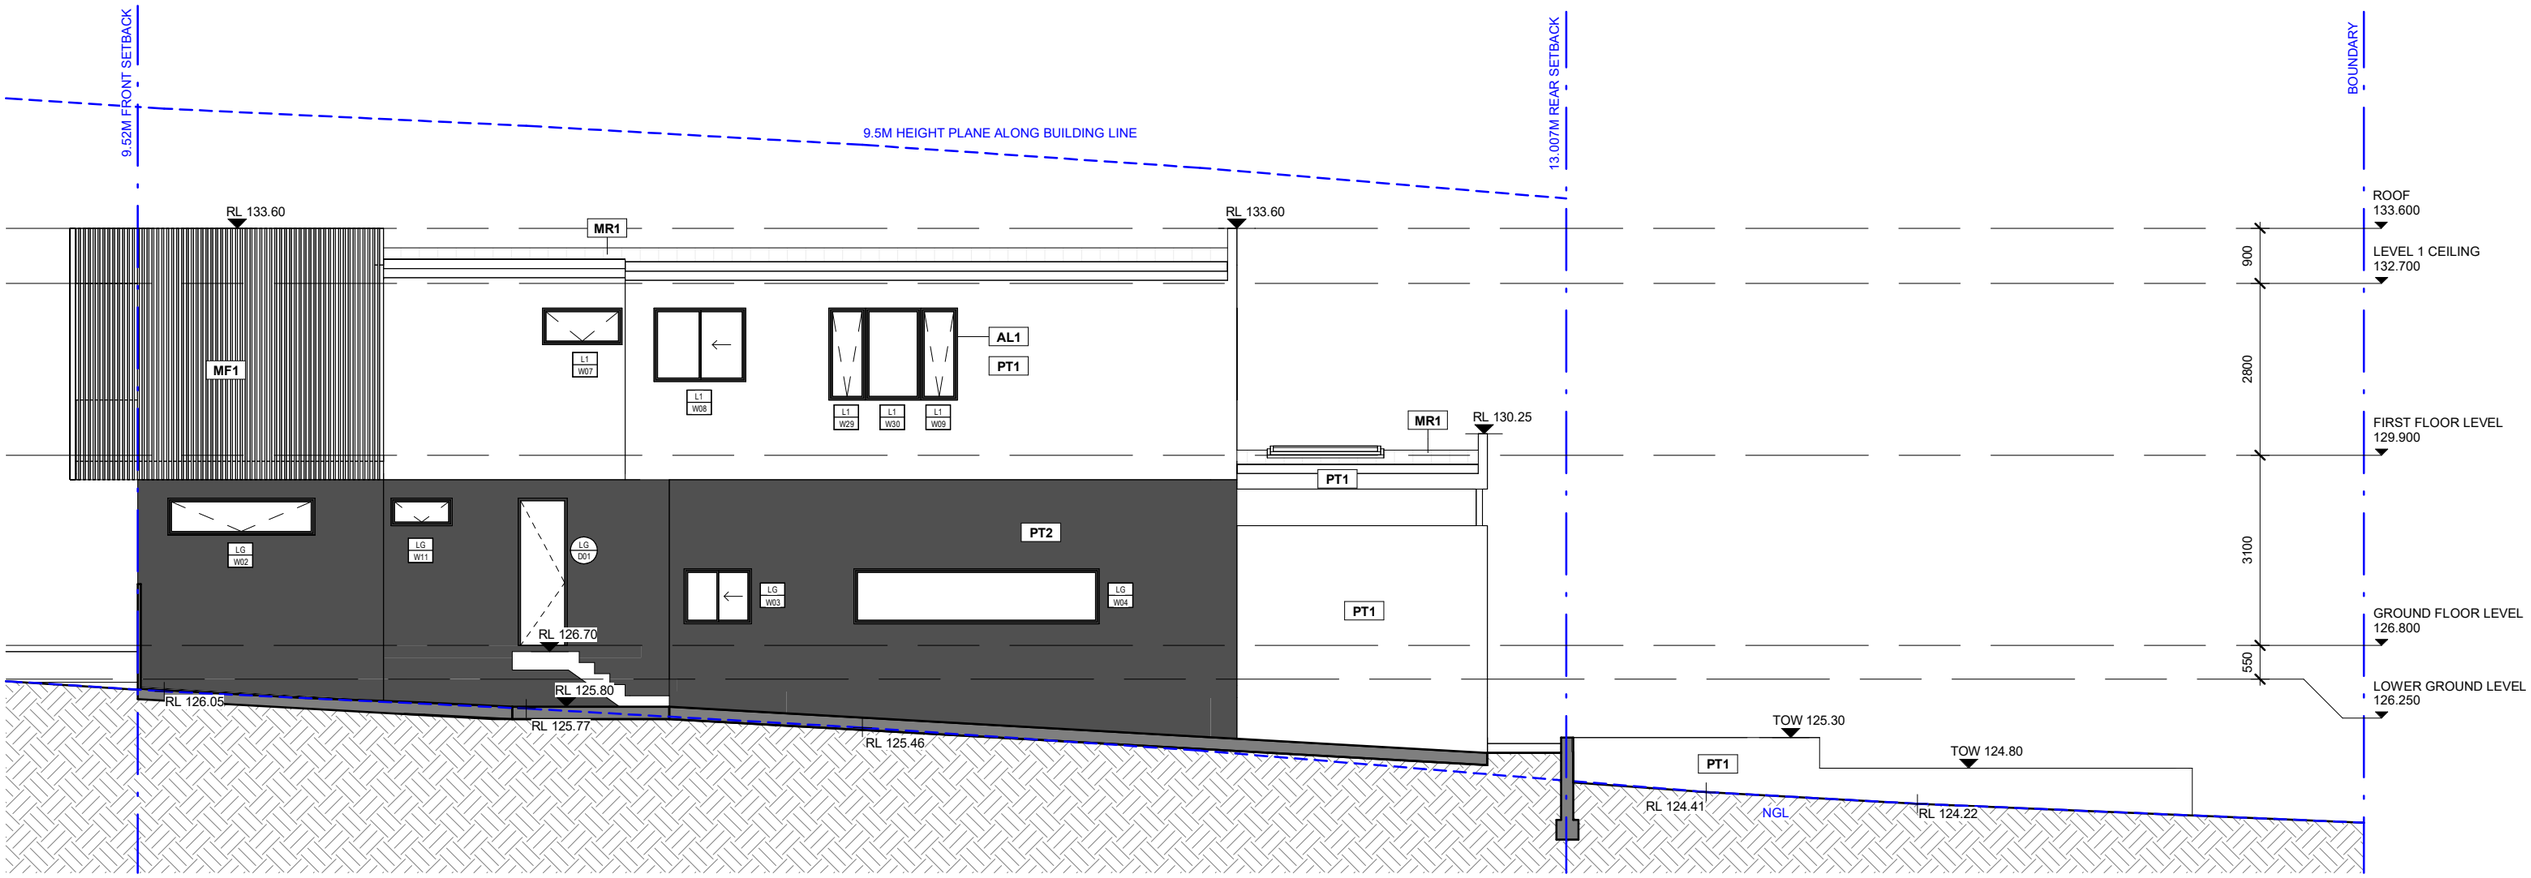

NOTES

- ALL WORKS TO BE IN ACCORDANCE WITH THE BUILDING CODE OF AUSTRALIA, AUSTRALIAN STANDARDS, STATUTORY REGULATIONS AND LOCAL AUTHORITY REQUIREMENTS.
- CONTRACTOR TO ENSURE CONSISTENCY BETWEEN SIMILAR MATERIAL IS MAINTAINED.
- PREPARE & MAKE GOOD ALL SURFACES & SUBSTRATE AS REQUIRED TO RECEIVE NEW FINISHES AS PER MANUFACTURER'S SPECIFICATION.
- ALL DIMENSIONS TO BE CHECKED ON SITE BEFORE COMMENCEMENT OF WORK. ALL DIMENSIONS MUST BE CHECKED & VERIFIED ON SITE PRIOR TO CONSTRUCTION & MANUFACTURE OF ANY ITEM.
- THIS DRAWING IS COPYRIGHT AND THE PROPERTY OF THE AUTHOR. IT MUST NOT BE RETAINED, COPIED OR USED WITHOUT THE EXPRESS AUTHORITY OF PLAY CO PTY LTD.

REV	DATE	DESCRIPTION
P1	19/09/25	PRELIMINARY PLAN
P2	08/12/25	PRELIMINARY PLAN
P3	21/01/26	PRELIMINARY PLAN
A	17/02/26	DA SUBMISSION
B	10/07/26	RFI
C	29/07/26	RFI

PROJECT

257 MARSDEN ROAD CARLINGFORD

ARCHITECT


PLAY CO ARCHITECTS
ARCHITECTURE | INTERIORS | PROJECT MANAGEMENT
PLAY CO PTY LTD

ABN 206 135 521 86
SUITE 801, 11 HELP STREET
CHATSWOOD NSW 2067
WWW.PLAY-CO.COM.AU
NOMINATED ARCHITECT
RAYMOND NG #8961
DESIGN PRACTITIONER DEP000234

CLIENT

PROJECT NUMBER	P632	PROJECT ADDRESS	257 MARSDEN ROAD CARLINGFORD
DRAWING NUMBER	A303	DRAWING TITLE	EAST ELEVATION

SCALE	1 : 100	PAPER SIZE	A3	REVISION	C
DRAWN BY	TT	REVIEWED BY	RN	STATUS	RFI

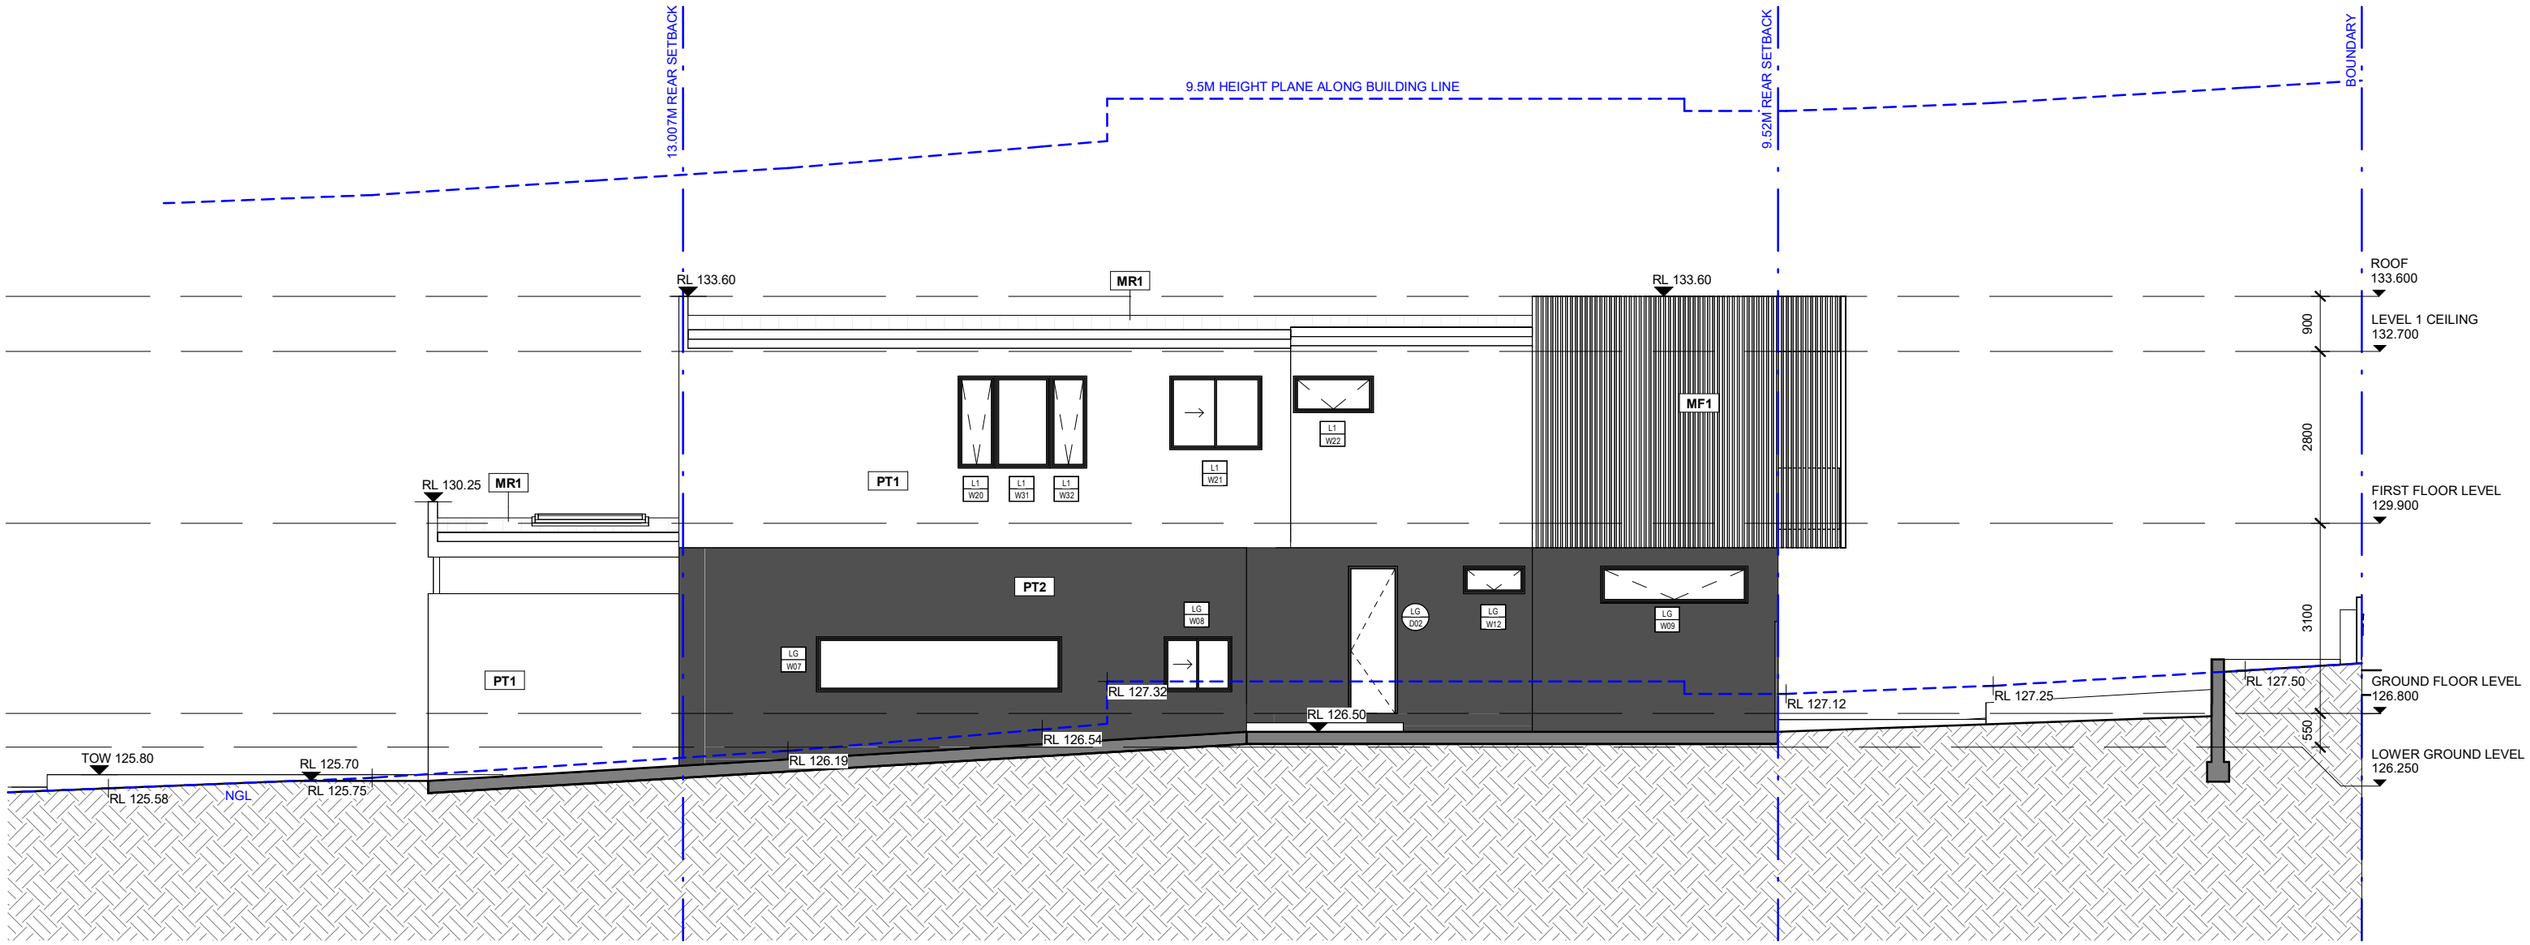

NOTES

- ALL WORKS TO BE IN ACCORDANCE WITH THE BUILDING CODE OF AUSTRALIA, AUSTRALIAN STANDARDS, STATUTORY REGULATIONS AND LOCAL AUTHORITY REQUIREMENTS.
- CONTRACTOR TO ENSURE CONSISTENCY BETWEEN SIMILAR MATERIAL IS MAINTAINED.
- PREPARE & MAKE GOOD ALL SURFACES & SUBSTRATE AS REQUIRED TO RECEIVE NEW FINISHES AS PER MANUFACTURER'S SPECIFICATION.
- ALL DIMENSIONS TO BE CHECKED ON SITE BEFORE COMMENCEMENT OF WORK. ALL DIMENSIONS MUST BE CHECKED & VERIFIED ON SITE PRIOR TO CONSTRUCTION & MANUFACTURE OF ANY ITEM.
- THIS DRAWING IS COPYRIGHT AND THE PROPERTY OF THE AUTHOR. IT MUST NOT BE RETAINED, COPIED OR USED WITHOUT THE EXPRESS AUTHORITY OF PLAY CO PTY LTD.

REV	DATE	DESCRIPTION
P1	19/09/25	PRELIMINARY PLAN
P2	08/12/25	PRELIMINARY PLAN
P3	21/01/26	PRELIMINARY PLAN
A	17/02/26	DA SUBMISSION
B	10/07/26	RFI
C	29/07/26	RFI

PROJECT

257 MARSDEN ROAD CARLINGFORD


ARCHITECT

PLAY CO ARCHITECTS
ARCHITECTURE | INTERIORS | PROJECT MANAGEMENT
PLAY CO PTY LTD
ABN 206 135 521 86
SUITE 801, 11 HELP STREET
CHATSWOOD NSW 2067
WWW.PLAY-CO.COM.AU
NOMINATED ARCHITECT
RAYMOND NG #8961
DESIGN PRACTITIONER DEP000234

CLIENT

PROJECT NUMBER	P632	PROJECT ADDRESS	257 MARSDEN ROAD CARLINGFORD
DRAWING NUMBER	A304	DRAWING TITLE	WEST ELEVATION

SCALE	1 : 100	PAPER SIZE	A3	REVISION	C
DRAWN BY	TT	REVIEWED BY	RN	STATUS	RFI

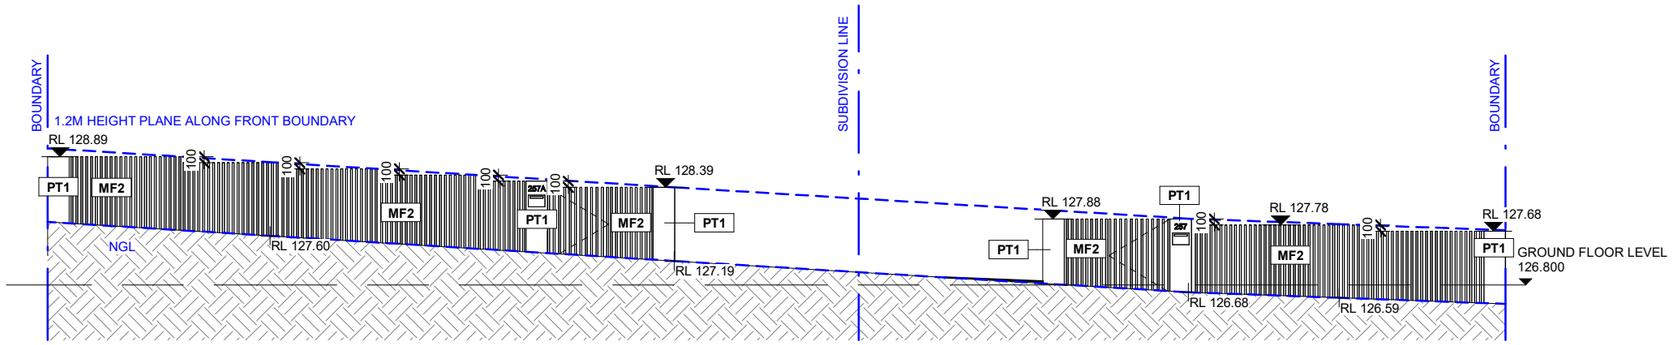

NOTES

- ALL WORKS TO BE IN ACCORDANCE WITH THE BUILDING CODE OF AUSTRALIA, AUSTRALIAN STANDARDS, STATUTORY REGULATIONS AND LOCAL AUTHORITY REQUIREMENTS.
- CONTRACTOR TO ENSURE CONSISTENCY BETWEEN SIMILAR MATERIAL IS MAINTAINED.
- PREPARE & MAKE GOOD ALL SURFACES & SUBSTRATE AS REQUIRED TO RECEIVE NEW FINISHES AS PER MANUFACTURER'S SPECIFICATION.
- ALL DIMENSIONS TO BE CHECKED ON SITE BEFORE COMMENCEMENT OF WORK. ALL DIMENSIONS MUST BE CHECKED & VERIFIED ON SITE PRIOR TO CONSTRUCTION & MANUFACTURE OF ANY ITEM.
- THIS DRAWING IS COPYRIGHT AND THE PROPERTY OF THE AUTHOR. IT MUST NOT BE RETAINED, COPIED OR USED WITHOUT THE EXPRESS AUTHORITY OF PLAY CO PTY LTD.

REV	DATE	DESCRIPTION
P1	19/09/25	PRELIMINARY PLAN
P2	08/12/25	PRELIMINARY PLAN
P3	21/01/26	PRELIMINARY PLAN
A	17/02/26	DA SUBMISSION
B	10/07/26	RFI
C	29/07/26	RFI

PROJECT

257 MARSDEN ROAD CARLINGFORD


ARCHITECT

PLAY CO ARCHITECTS
ARCHITECTURE | INTERIORS | PROJECT MANAGEMENT
PLAY CO PTY LTD
ABN 206 135 521 86
SUITE 801, 11 HELP STREET
CHATSWOOD NSW 2067
WWW.PLAY-CO.COM.AU
NOMINATED ARCHITECT
RAYMOND NG #8961
DESIGN PRACTITIONER DEP000234

CLIENT

PROJECT NUMBER	P632	PROJECT ADDRESS	257 MARSDEN ROAD CARLINGFORD
DRAWING NUMBER	A305	DRAWING TITLE	SOUTH FENCE ELEVATION

SCALE	1 : 100	PAPER SIZE	A3	REVISION	C
DRAWN BY	TT	REVIEWED BY	RN	STATUS	RFI

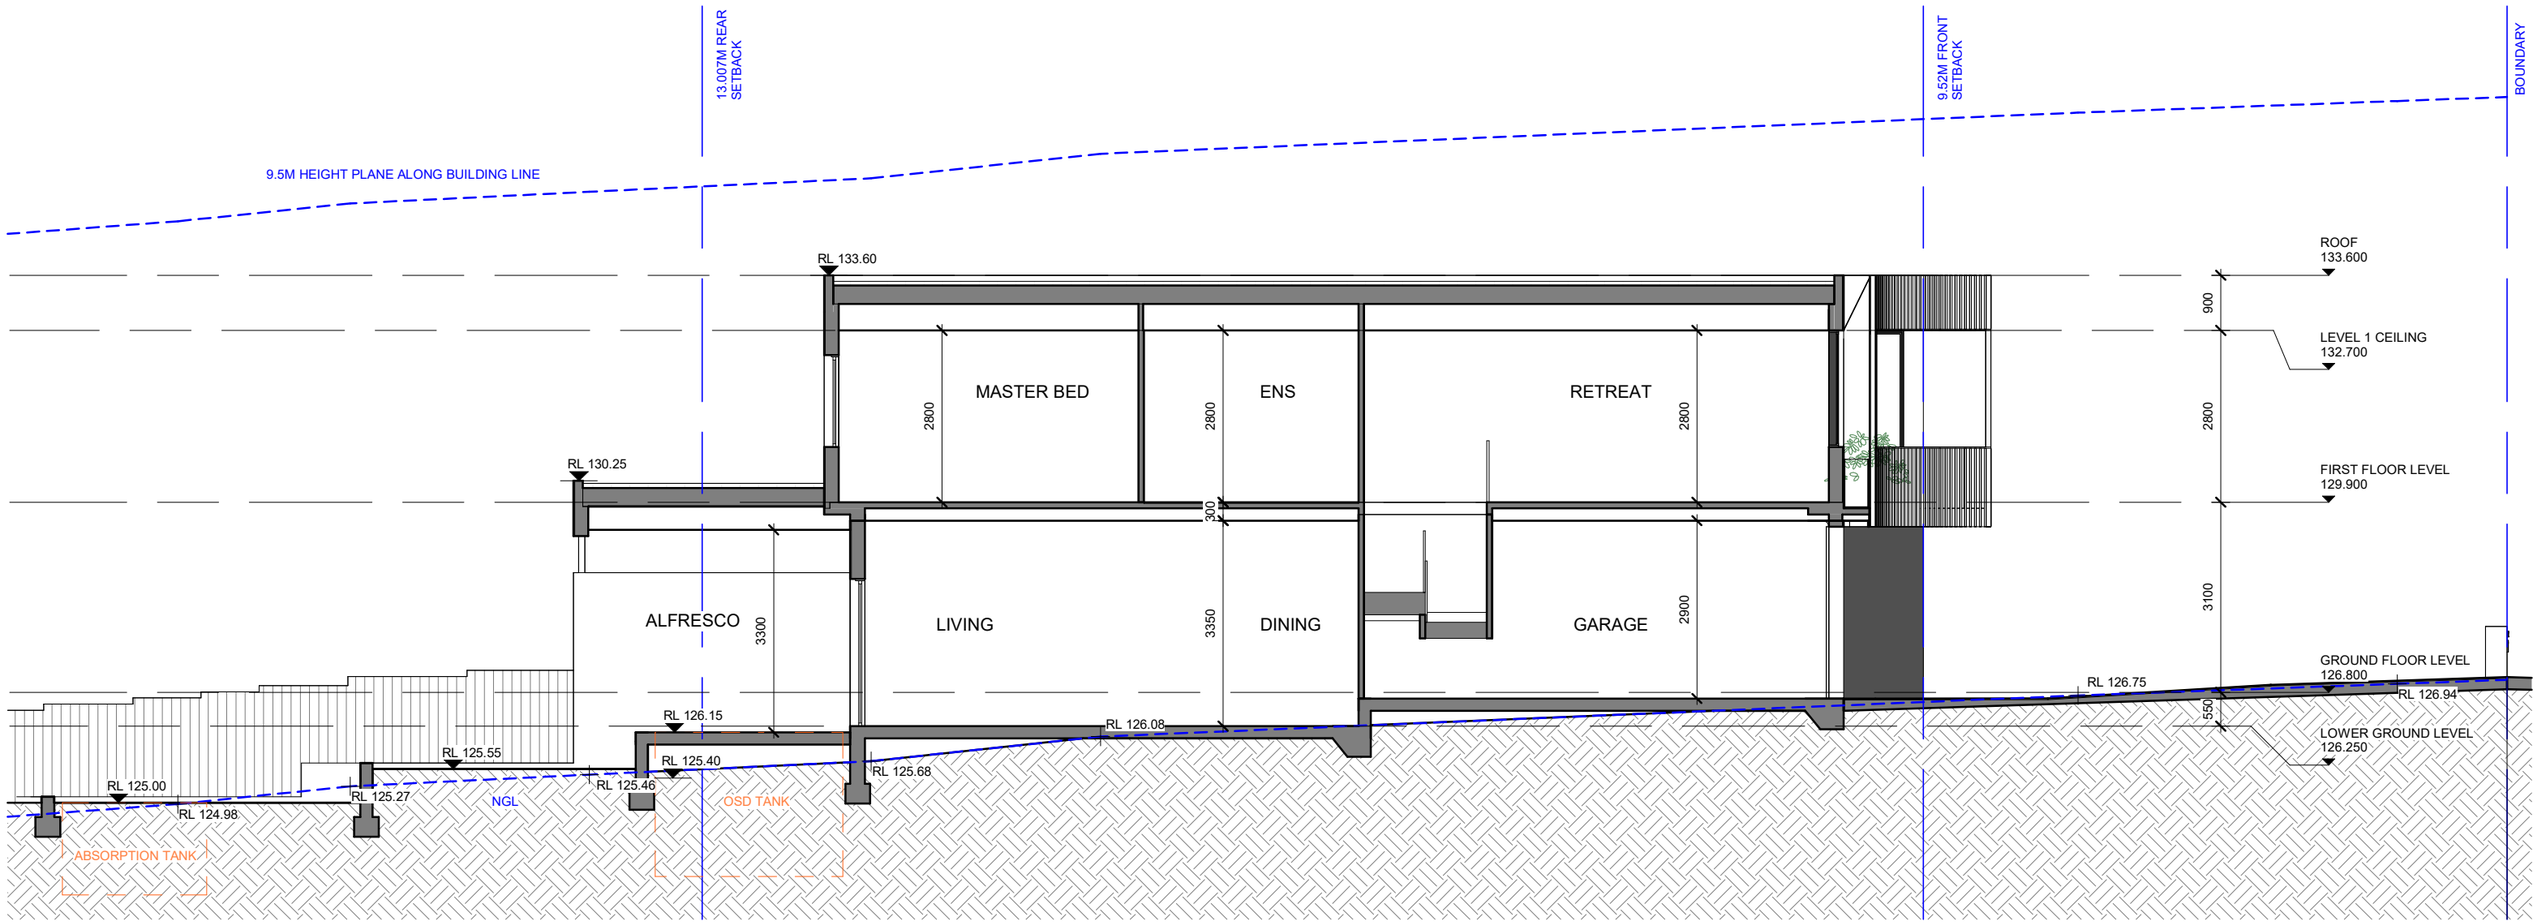

STRUCTURE NOTE

FLOOR:
CONCRETE (GROUND FLOOR)
TIMBER FRAME WITH 75MM HEBEL (FIRST FLOOR)

EXTERNAL WALL:
TIMBER FRAME WITH 75MM HEBEL (BOTH FLOORS)

INTERNAL WALL:
TIMBER STUD (BOTH FLOORS)

ROOF:
TIMBER FRAME WITH METAL ROOF

COLOUR NOTE

EXTERNAL WALL:
DARK TONE (GROUND FLOOR)
LIGHT TONE (FIRST FLOOR)

ROOF:
MEDIUM TONE

NOTES

- ALL WORKS TO BE IN ACCORDANCE WITH THE BUILDING CODE OF AUSTRALIA, AUSTRALIAN STANDARDS, STATUTORY REGULATIONS AND LOCAL AUTHORITY REQUIREMENTS.
- CONTRACTOR TO ENSURE CONSISTENCY BETWEEN SIMILAR MATERIAL IS MAINTAINED.
- PREPARE & MAKE GOOD ALL SURFACES & SUBSTRATE AS REQUIRED TO RECEIVE NEW FINISHES AS PER MANUFACTURER'S SPECIFICATION.
- ALL DIMENSIONS TO BE CHECKED ON SITE BEFORE COMMENCEMENT OF WORK. ALL DIMENSIONS MUST BE CHECKED & VERIFIED ON SITE PRIOR TO CONSTRUCTION & MANUFACTURE OF ANY ITEM.
- THIS DRAWING IS COPYRIGHT AND THE PROPERTY OF THE AUTHOR. IT MUST NOT BE RETAINED, COPIED OR USED WITHOUT THE EXPRESS AUTHORITY OF PLAY CO PTY LTD.

REV	DATE	DESCRIPTION
P1	19/09/25	PRELIMINARY PLAN
P2	08/12/25	PRELIMINARY PLAN
P3	21/01/26	PRELIMINARY PLAN
A	17/02/26	DA SUBMISSION
B	10/07/26	RFI
C	29/07/26	RFI


PROJECT
257 MARSDEN ROAD CARLINGFORD

ARCHITECT

PLAY CO ARCHITECTS
PLAY CO PTY LTD
ABN 206 135 521 86
SUITE 801, 11 HELP STREET
CHATSWOOD NSW 2067
WWW.PLAY-CO.COM.AU
NOMINATED ARCHITECT
RAYMOND NG #8961
DESIGN PRACTITIONER DEP000234

CLIENT

PROJECT NUMBER	P632	PROJECT ADDRESS	257 MARSDEN ROAD CARLINGFORD
DRAWING NUMBER	A401	DRAWING TITLE	PROPOSED SECTION A
SCALE	1 : 100	PAPER SIZE	A3
REVISION	C		
DRAWN BY	TT	REVIEWED BY	RN
STATUS	RFI		

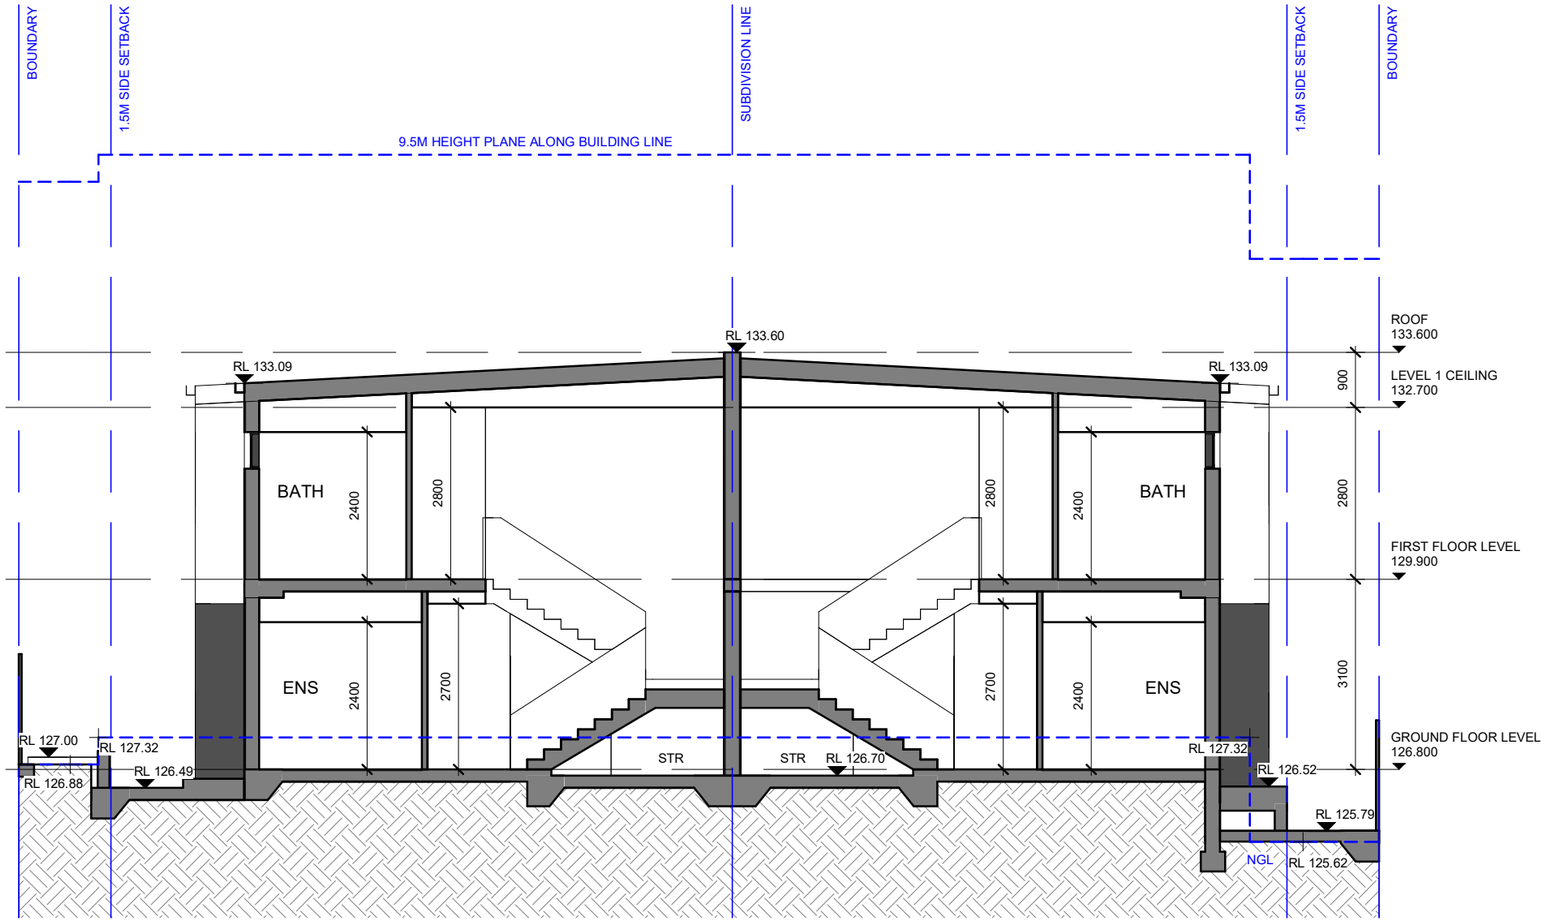

STRUCTURE NOTE

FLOOR:
CONCRETE (GROUND FLOOR)
TIMBER FRAME WITH 75MM HEBEL (FIRST FLOOR)

EXTERNAL WALL:
TIMBER FRAME WITH 75MM HEBEL (BOTH FLOORS)

INTERNAL WALL:
TIMBER STUD (BOTH FLOORS)

ROOF:
TIMBER FRAME WITH METAL ROOF

COLOUR NOTE

EXTERNAL WALL:
DARK TONE (GROUND FLOOR)
LIGHT TONE (FIRST FLOOR)

ROOF:
MEDIUM TONE

NOTES

- ALL WORKS TO BE IN ACCORDANCE WITH THE BUILDING CODE OF AUSTRALIA, AUSTRALIAN STANDARDS, STATUTORY REGULATIONS AND LOCAL AUTHORITY REQUIREMENTS.
- CONTRACTOR TO ENSURE CONSISTENCY BETWEEN SIMILAR MATERIAL IS MAINTAINED.
- PREPARE & MAKE GOOD ALL SURFACES & SUBSTRATE AS REQUIRED TO RECEIVE NEW FINISHES AS PER MANUFACTURER'S SPECIFICATION.
- ALL DIMENSIONS TO BE CHECKED ON SITE BEFORE COMMENCEMENT OF WORK. ALL DIMENSIONS MUST BE CHECKED & VERIFIED ON SITE PRIOR TO CONSTRUCTION & MANUFACTURE OF ANY ITEM.
- THIS DRAWING IS COPYRIGHT AND THE PROPERTY OF THE AUTHOR. IT MUST NOT BE RETAINED, COPIED OR USED WITHOUT THE EXPRESS AUTHORITY OF PLAY CO PTY LTD.

REV	DATE	DESCRIPTION
P1	19/09/25	PRELIMINARY PLAN
P2	08/12/25	PRELIMINARY PLAN
P3	21/01/26	PRELIMINARY PLAN
A	17/02/26	DA SUBMISSION
B	10/07/26	RFI
C	29/07/26	RFI


PROJECT
257 MARSDEN ROAD CARLINGFORD

ARCHITECT

PLAY CO ARCHITECTS
PLAY CO PTY LTD
ABN 206 135 521 86
SUITE 801, 11 HELP STREET
CHATSWOOD NSW 2067
WWW.PLAY-CO.COM.AU
NOMINATED ARCHITECT
RAYMOND NG #8961
DESIGN PRACTITIONER DEP000234


CLIENT

PROJECT NUMBER	P632	PROJECT ADDRESS	257 MARSDEN ROAD CARLINGFORD
DRAWING NUMBER	A402	DRAWING TITLE	PROPOSED SECTION B
SCALE	1 : 100	PAPER SIZE	A3
DRAWN BY	TT	REVIEWED BY	RN
		REVISION	C
		STATUS	RFI

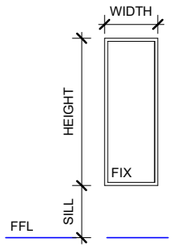


WINDOW TYPE A

NUMBER	WIDTH	HEIGHT	SILL HEIGHT	NOTES
LG W04	4000	900	900	FIXED
LG W07	4000	900	900	FIXED
L1 W01	1050	1900	900	FIXED
L1 W03	1200	1900	900	FIXED
L1 W04	1400	1900	900	FIXED
L1 W25	1400	1900	900	FIXED
L1 W27	1050	1900	900	FIXED
L1 W28	1050	1900	900	FIXED
L1 W30	900	1500	900	FIXED; FROST
L1 W31	900	1500	900	FIXED; FROST

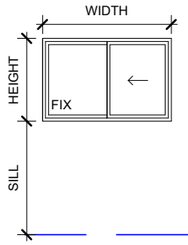


WINDOW TYPE B

NUMBER	WIDTH	HEIGHT	SILL HEIGHT	NOTES
LG W03	1100	900	900	LEFT SLIDER
LG W08	1100	900	900	RIGHT SLIDER
L1 W08	1500	1200	1200	LEFT SLIDER; FROST GLAZING; 125 LIMITER
L1 W21	1500	1200	1200	RIGHT SLIDER; FROST GLAZING; 125 LIMITER

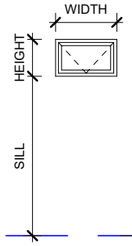


WINDOW TYPE C

NUMBER	WIDTH	HEIGHT	SILL HEIGHT	NOTES
LG W02	2400	600	1800	AWNING; 125 LIMITER
LG W09	2400	600	1800	AWNING; 125 LIMITER
LG W11	1000	450	1950	AWNING; FROST GLAZING; 125 LIMITER
LG W12	1000	450	1950	AWNING; FROST GLAZING; 125 LIMITER
L1 W02	1050	1900	900	AWNING; 125 LIMITER
L1 W07	1300	600	1800	AWNING; FROST GLAZING
L1 W09	600	1500	900	AWNING; 125 LIMITER
L1 W12	600	1500	900	AWNING; 125 LIMITER
L1 W17	600	1500	900	AWNING; 125 LIMITER
L1 W20	600	1500	900	AWNING; 125 LIMITER
L1 W22	1300	600	1800	AWNING; FROST GLAZING; 125 LIMITER
L1 W26	1050	1900	900	AWNING; FROST GLAZING; 125 LIMITER
L1 W29	600	1500	900	AWNING; 125 LIMITER
L1 W32	600	1500	900	AWNING; 125 LIMITER

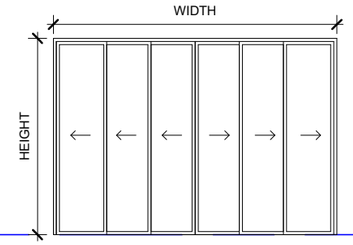


WINDOW TYPE D

NUMBER	WIDTH	HEIGHT	SILL HEIGHT	NOTES
LG W05	7000	2400	0	
LG W06	7000	2400	0	

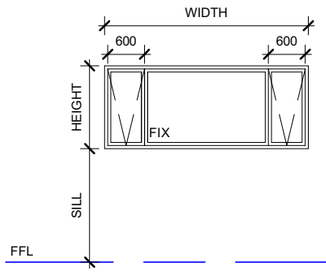


WINDOW TYPE E

NUMBER	WIDTH	HEIGHT	SILL HEIGHT	NOTES
LG W01	2100	1500	900	125 LIMITER TO AWNING
LG W10	2100	1500	900	125 LIMITER TO AWNING
L1 W10	2100	1500	900	125 LIMITER TO AWNING
L1 W14	2400	1500	900	125 LIMITER TO AWNING
L1 W15	2400	1500	900	125 LIMITER TO AWNING
L1 W19	2100	1500	900	125 LIMITER TO AWNING

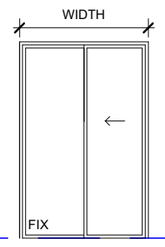

WINDOW TYPE F

NUMBER	WIDTH	HEIGHT	SILL HEIGHT	NOTES
L1 W06	2400	2800	0	RIGHT SLIDER
L1 W23	2400	2800	0	LEFT SLIDER

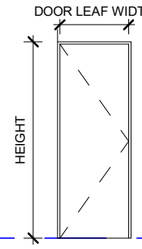


EXTERNAL DOORS
USE : EXTERNAL (LAUNDRY)

- FROSTED GLAZED DOOR
- POWDERCOATED ALUMINIUM FRAME
- PRIVACY LOCK

DOOR TYPE E

NUMBER	DOOR LEAF WIDTH	HEIGHT	NOTES
LG D01	720	2400	
LG D02	720	2400	

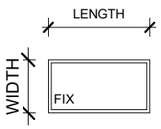

SKYLIGHT A

NUMBER	WIDTH	HEIGHT	NOTES
L1 W11	1800	1800	
L1 W13	1800	1800	
L1 W16	1800	1800	
L1 W18	1800	1800	

NOTES

- ALL WORKS TO BE IN ACCORDANCE WITH THE BUILDING CODE OF AUSTRALIA, AUSTRALIAN STANDARDS, STATUTORY REGULATIONS AND LOCAL AUTHORITY REQUIREMENTS.
- CONTRACTOR TO ENSURE CONSISTENCY BETWEEN SIMILAR MATERIAL IS MAINTAINED.
- PREPARE & MAKE GOOD ALL SURFACES & SUBSTRATE AS REQUIRED TO RECEIVE NEW FINISHES AS PER MANUFACTURER'S SPECIFICATION.
- ALL DIMENSIONS TO BE CHECKED ON SITE BEFORE COMMENCEMENT OF WORK. ALL DIMENSIONS MUST BE CHECKED & VERIFIED ON SITE PRIOR TO CONSTRUCTION & MANUFACTURE OF ANY ITEM.
- THIS DRAWING IS COPYRIGHT AND THE PROPERTY OF THE AUTHOR. IT MUST NOT BE RETAINED, COPIED OR USED WITHOUT THE EXPRESS AUTHORITY OF PLAY CO PTY LTD.

REV	DATE	DESCRIPTION
P1	19/09/25	PRELIMINARY PLAN
P2	08/12/25	PRELIMINARY PLAN
P3	21/01/26	PRELIMINARY PLAN
A	17/02/26	DA SUBMISSION
B	10/07/26	RFI
C	29/07/26	RFI

PROJECT


257 MARSDEN ROAD CARLINGFORD

ARCHITECT

PLAY CO ARCHITECTS
ARCHITECTURE | INTERIORS | PROJECT MANAGEMENT
PLAY CO PTY LTD
ABN 206 135 521 86
SUITE 801, 11 HELP STREET
CHATSWOOD NSW 2067
WWW.PLAY-CO.COM.AU
NOMINATED ARCHITECT
RAYMOND NG #8961
DESIGN PRACTITIONER DEP000234

CLIENT

PROJECT NUMBER	P632	PROJECT ADDRESS	257 MARSDEN ROAD CARLINGFORD
DRAWING NUMBER	A411	DRAWING TITLE	WINDOW AND DOOR SCHEDULE
SCALE	1 : 100	PAPER SIZE	A3
DRAWN BY	TT	REVIEWED BY	RN
REVISION	C	STATUS	RFI

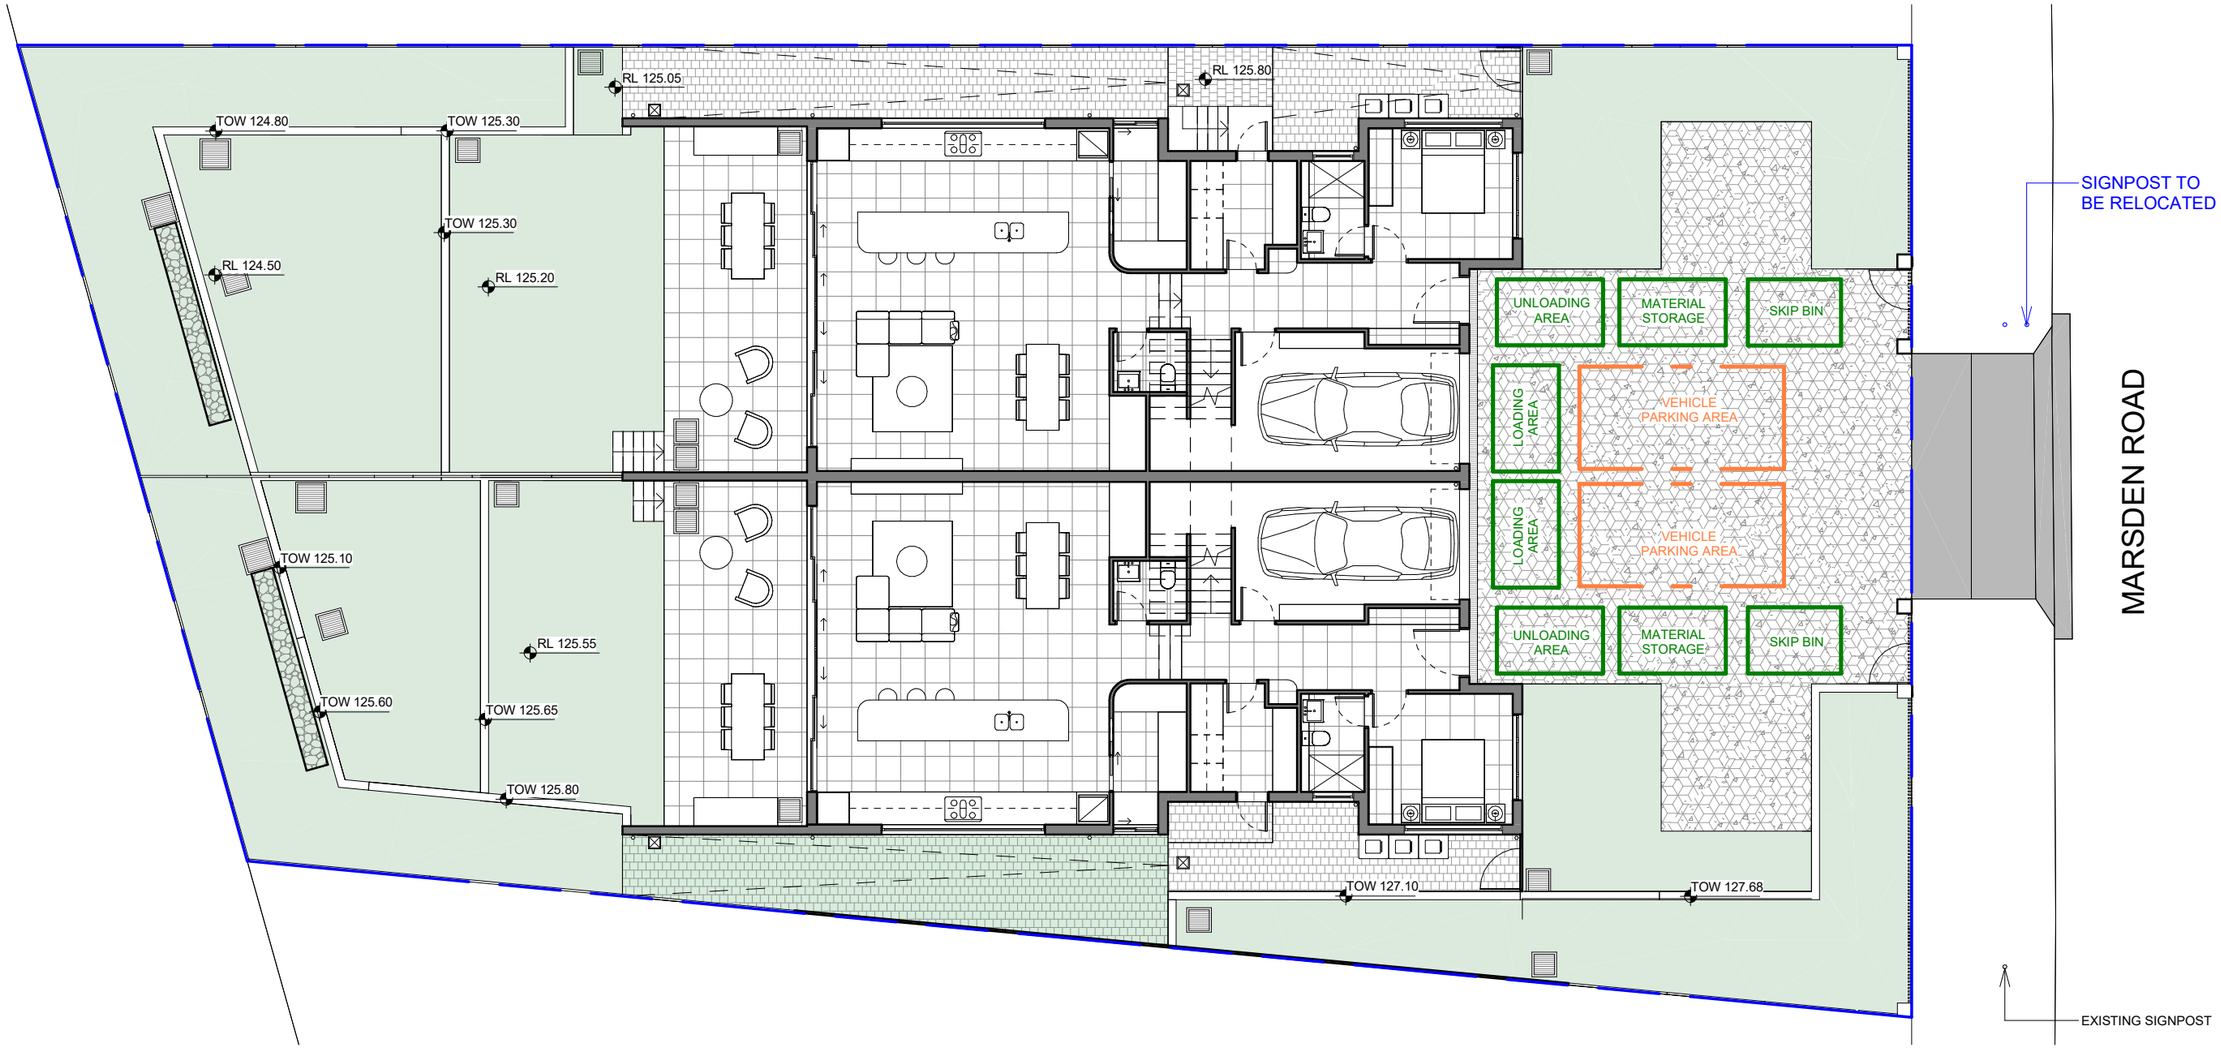

NOTES

- ALL WORKS TO BE IN ACCORDANCE WITH THE BUILDING CODE OF AUSTRALIA, AUSTRALIAN STANDARDS, STATUTORY REGULATIONS AND LOCAL AUTHORITY REQUIREMENTS.
- CONTRACTOR TO ENSURE CONSISTENCY BETWEEN SIMILAR MATERIAL IS MAINTAINED.
- PREPARE & MAKE GOOD ALL SURFACES & SUBSTRATE AS REQUIRED TO RECEIVE NEW FINISHES AS PER MANUFACTURER'S SPECIFICATION.
- ALL DIMENSIONS TO BE CHECKED ON SITE BEFORE COMMENCEMENT OF WORK. ALL DIMENSIONS MUST BE CHECKED & VERIFIED ON SITE PRIOR TO CONSTRUCTION & MANUFACTURE OF ANY ITEM.
- THIS DRAWING IS COPYRIGHT AND THE PROPERTY OF THE AUTHOR. IT MUST NOT BE RETAINED, COPIED OR USED WITHOUT THE EXPRESS AUTHORITY OF PLAY CO PTY LTD.

REV	DATE	DESCRIPTION
P1	19/09/25	PRELIMINARY PLAN
P2	08/12/25	PRELIMINARY PLAN
P3	21/01/26	PRELIMINARY PLAN
A	17/02/26	DA SUBMISSION
B	10/07/26	RFI
C	29/07/26	RFI

PROJECT


257 MARSDEN ROAD CARLINGFORD

ARCHITECT

PLAY CO ARCHITECTS
ARCHITECTURE | INTERIORS | PROJECT MANAGEMENT
PLAY CO PTY LTD
ABN 206 135 521 86
SUITE 801, 11 HELP STREET
CHATSWOOD NSW 2067
WWW.PLAY-CO.COM.AU
NOMINATED ARCHITECT
RAYMOND NG #8961
DESIGN PRACTITIONER DEP000234

CLIENT

PROJECT NUMBER	P632	PROJECT ADDRESS	257 MARSDEN ROAD CARLINGFORD		
DRAWING NUMBER	A420	DRAWING TITLE	CONSTRUCTION MANAGEMENT PLAN		
SCALE	1 : 150	PAPER SIZE	A3	REVISION	C
DRAWN BY	TT	REVIEWED BY	RN	STATUS	RFI

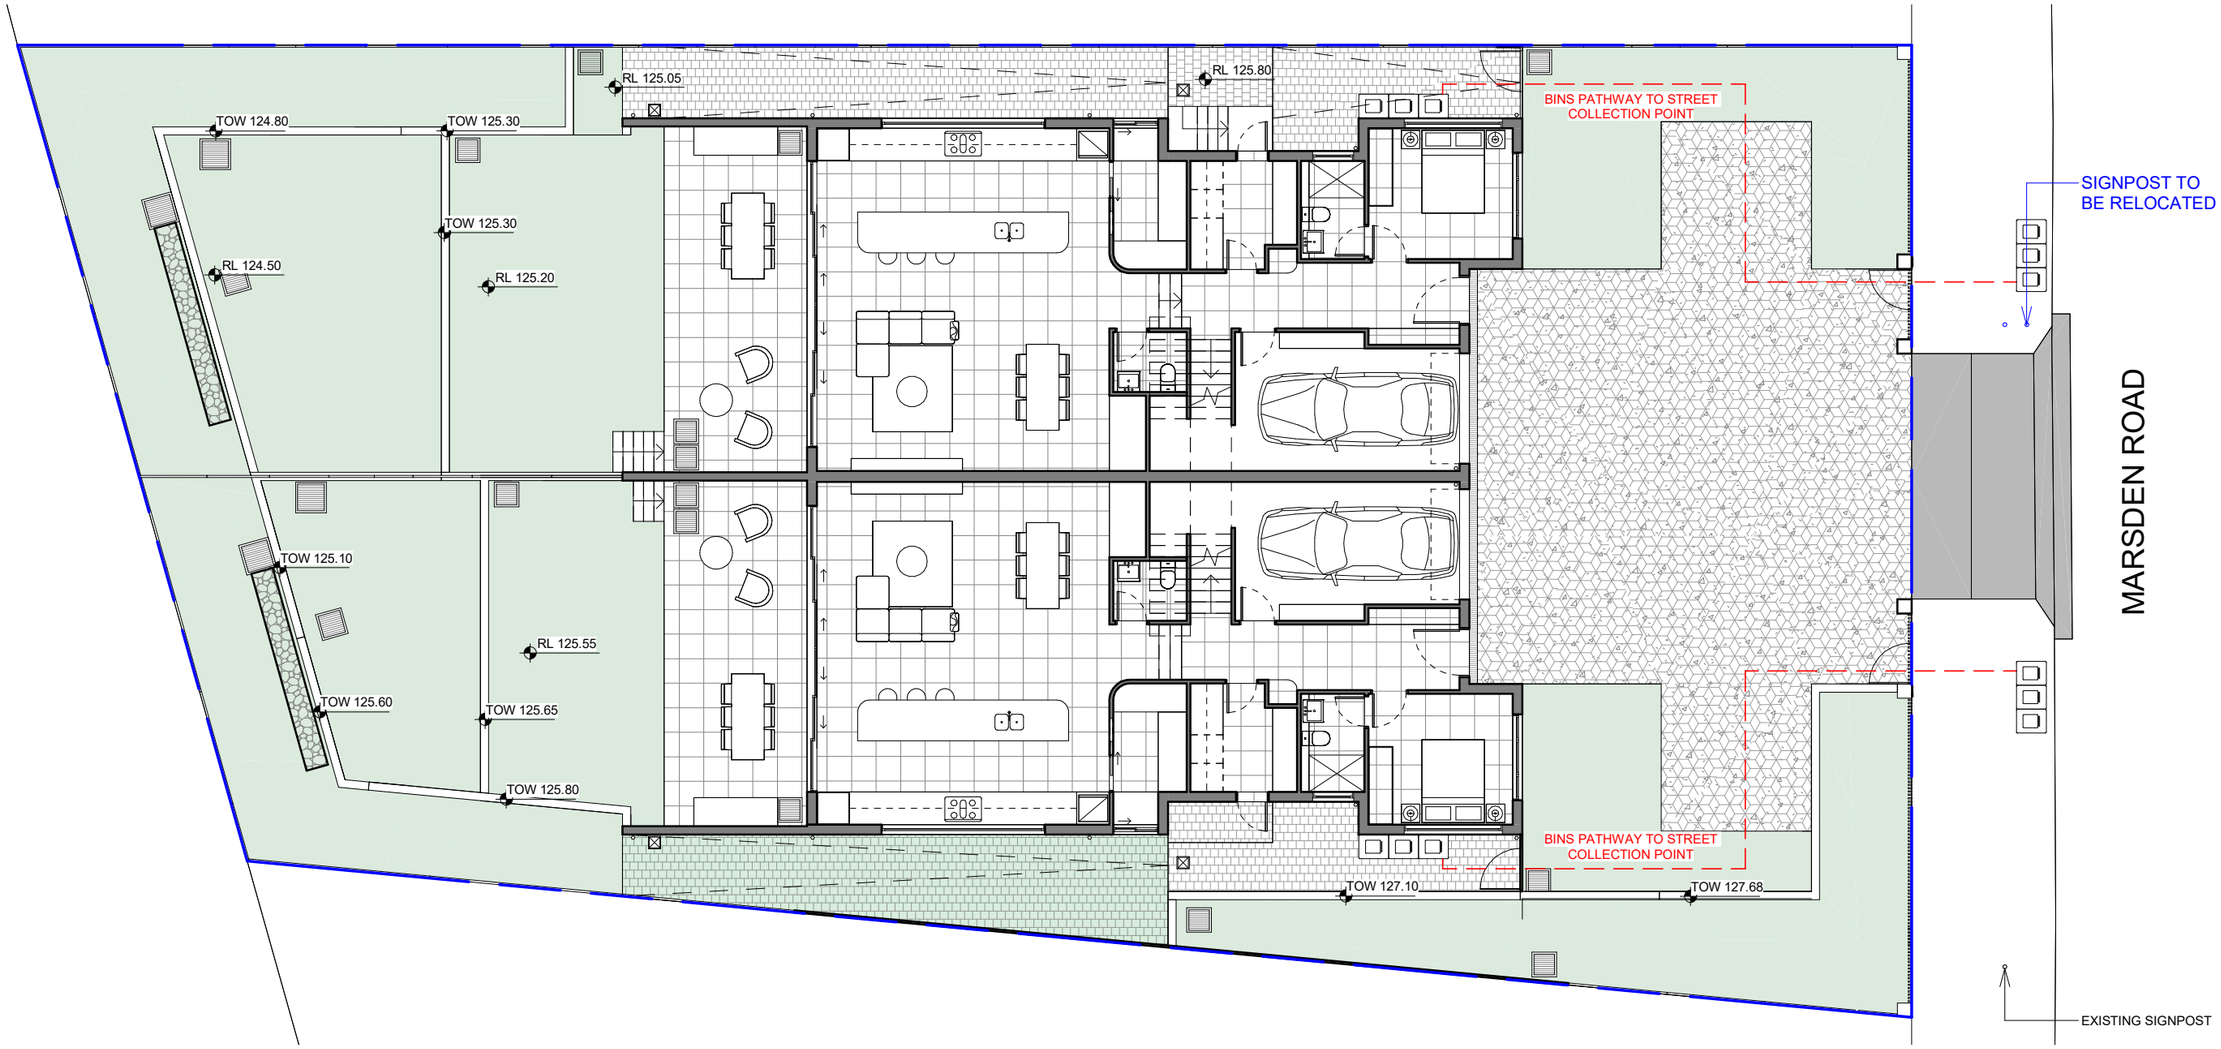

NOTES

- ALL WORKS TO BE IN ACCORDANCE WITH THE BUILDING CODE OF AUSTRALIA, AUSTRALIAN STANDARDS, STATUTORY REGULATIONS AND LOCAL AUTHORITY REQUIREMENTS.
- CONTRACTOR TO ENSURE CONSISTENCY BETWEEN SIMILAR MATERIAL IS MAINTAINED.
- PREPARE & MAKE GOOD ALL SURFACES & SUBSTRATE AS REQUIRED TO RECEIVE NEW FINISHES AS PER MANUFACTURER'S SPECIFICATION.
- ALL DIMENSIONS TO BE CHECKED ON SITE BEFORE COMMENCEMENT OF WORK. ALL DIMENSIONS MUST BE CHECKED & VERIFIED ON SITE PRIOR TO CONSTRUCTION & MANUFACTURE OF ANY ITEM.
- THIS DRAWING IS COPYRIGHT AND THE PROPERTY OF THE AUTHOR. IT MUST NOT BE RETAINED, COPIED OR USED WITHOUT THE EXPRESS AUTHORITY OF PLAY CO PTY LTD.

REV	DATE	DESCRIPTION
P1	19/09/25	PRELIMINARY PLAN
P2	08/12/25	PRELIMINARY PLAN
P3	21/01/26	PRELIMINARY PLAN
A	17/02/26	DA SUBMISSION
B	10/07/26	RFI
C	29/07/26	RFI

PROJECT


257 MARSDEN ROAD CARLINGFORD

ARCHITECT

PLAY CO ARCHITECTS
ARCHITECTURE | INTERIORS | PROJECT MANAGEMENT
PLAY CO PTY LTD
ABN 206 135 521 86
SUITE 801, 11 HELP STREET
CHATSWOOD NSW 2067
WWW.PLAY-CO.COM.AU
NOMINATED ARCHITECT
RAYMOND NG #8961
DESIGN PRACTITIONER DEP000234


CLIENT

PROJECT NUMBER	P632	PROJECT ADDRESS	257 MARSDEN ROAD CARLINGFORD		
DRAWING NUMBER	A421	DRAWING TITLE	WASTE MANAGEMENT PLAN		
SCALE	1 : 150	PAPER SIZE	A3	REVISION	C
DRAWN BY	TT	REVIEWED BY	RN	STATUS	RFI

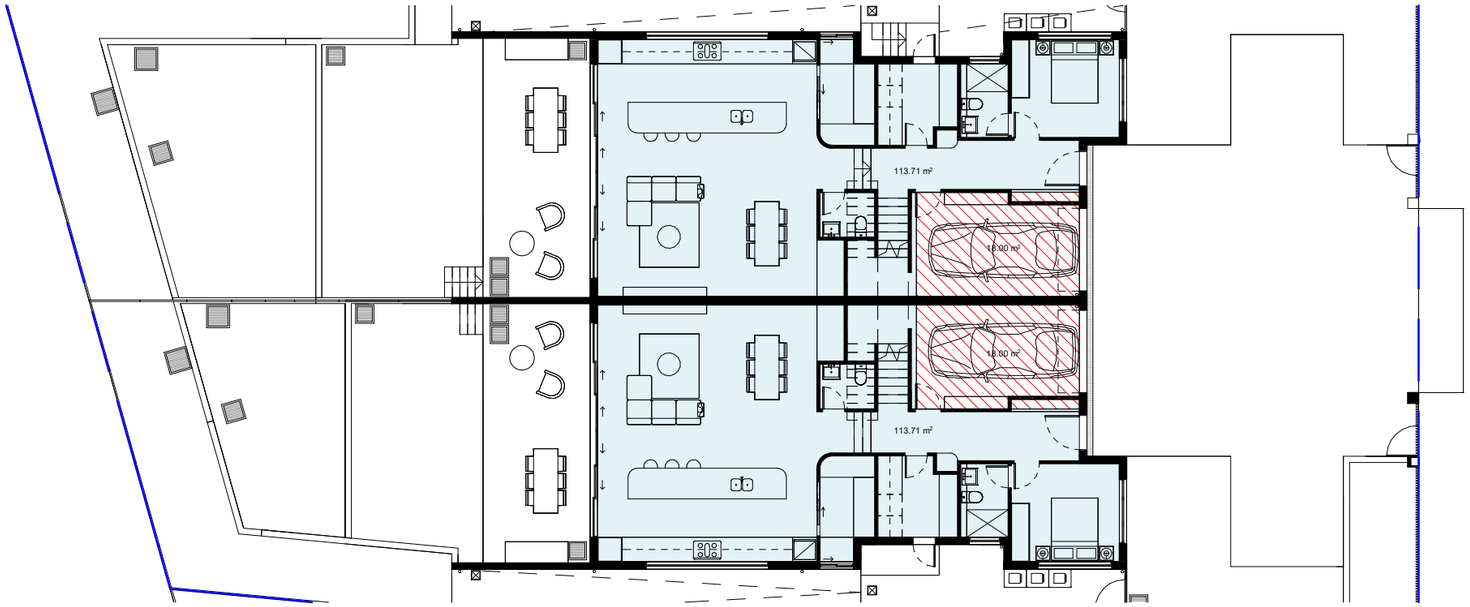

1 GROUND LEVEL GFA

1 : 200

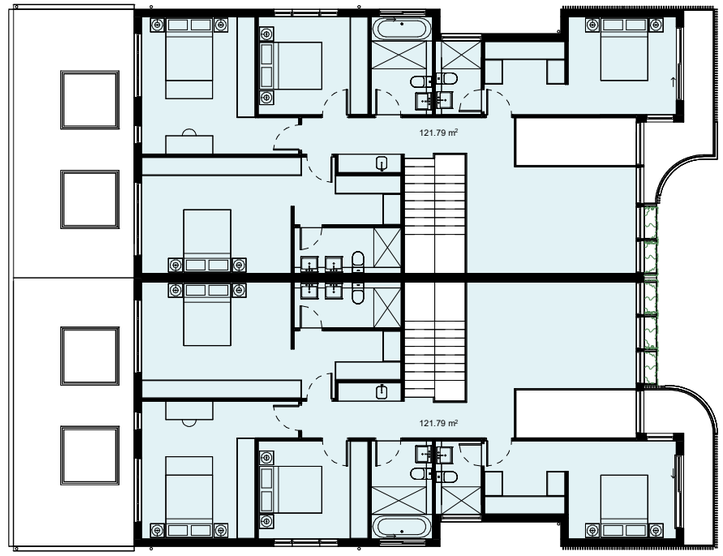

2 LEVEL 1 GFA

1 : 200

SITE DATA			
SITE AREA	942.20 m²		
ZONING	R2		
MAX GFA	471.10 m²		
PROPOSED AREA - LOT 1 (No. 257)		**PROPOSED AREA - LOT 2 (No. 257A)**	
GROUND FLOOR	113.71 m²	GROUND FLOOR	113.71 m²
LEVEL 1	121.79 m²	LEVEL 1	121.79 m²
TOTAL	235.50 m²	TOTAL	235.50 m²
TOTAL PROPOSED AREA			471.00 m²

COMPLIANCE TABLE		
CONTROL	REQUIRED	PROPOSED
SITE AREA	400.00 m²	942.20 m²
PRIMARY RD SETBACK	9.52 m	9.52 m
SIDE SETBACK - GF	0.90 m	0.90 m
SIDE SETBACK - L1	1.90 m	1.90 m
REAR SETBACK - GF	3.00 m	3.00 m
REAR SETBACK - L1	8.00 m	8.00 m
MIN LANDSCAPED AREA	376.88 m²	341.47 m²
- FORWARD OF THE BUILDING LINE	0.00 m²	83.38 m²
- BEHIND OF THE BUILDING LINE	188.44 m²	258.09 m²
MIN DEEP SOIL	282.66 m²	209.59 m²
- FORWARD OF THE BUILDING LINE	56.53 m²	49.17 m²
- BEHIND OF THE BUILDING LINE	141.33 m²	160.42 m²
NUMBER OF PARKING	1	2

NOTES

- ALL WORKS TO BE IN ACCORDANCE WITH THE BUILDING CODE OF AUSTRALIA, AUSTRALIAN STANDARDS, STATUTORY REGULATIONS AND LOCAL AUTHORITY REQUIREMENTS.
- CONTRACTOR TO ENSURE CONSISTENCY BETWEEN SIMILAR MATERIAL IS MAINTAINED.
- PREPARE & MAKE GOOD ALL SURFACES & SUBSTRATE AS REQUIRED TO RECEIVE NEW FINISHES AS PER MANUFACTURER'S SPECIFICATION.
- ALL DIMENSIONS TO BE CHECKED ON SITE BEFORE COMMENCEMENT OF WORK. ALL DIMENSIONS MUST BE CHECKED & VERIFIED ON SITE PRIOR TO CONSTRUCTION & MANUFACTURE OF ANY ITEM.
- THIS DRAWING IS COPYRIGHT AND THE PROPERTY OF THE AUTHOR. IT MUST NOT BE RETAINED, COPIED OR USED WITHOUT THE EXPRESS AUTHORITY OF PLAY CO PTY LTD.

REV	DATE	DESCRIPTION
P1	19/09/25	PRELIMINARY PLAN
P2	08/12/25	PRELIMINARY PLAN
P3	21/01/26	PRELIMINARY PLAN
A	17/02/26	DA SUBMISSION
B	10/07/26	RFI
C	29/07/26	RFI

PROJECT


257 MARSDEN ROAD CARLINGFORD

ARCHITECT

PLAY CO ARCHITECTS
ARCHITECTURE | INTERIORS | PROJECT MANAGEMENT
PLAY CO PTY LTD
ABN 206 135 521 86
SUITE 801, 11 HELP STREET
CHATSWOOD NSW 2067
WWW.PLAY-CO.COM.AU
NOMINATED ARCHITECT
RAYMOND NG #8961
DESIGN PRACTITIONER DEP000234

CLIENT

PROJECT NUMBER	P632	PROJECT ADDRESS	257 MARSDEN ROAD CARLINGFORD
DRAWING NUMBER	A500	DRAWING TITLE	GFA DIAGRAM
SCALE	1 : 200	PAPER SIZE	A3
DRAWN BY	TT	REVIEWED BY	RN
REVISION	C	STATUS	RFI

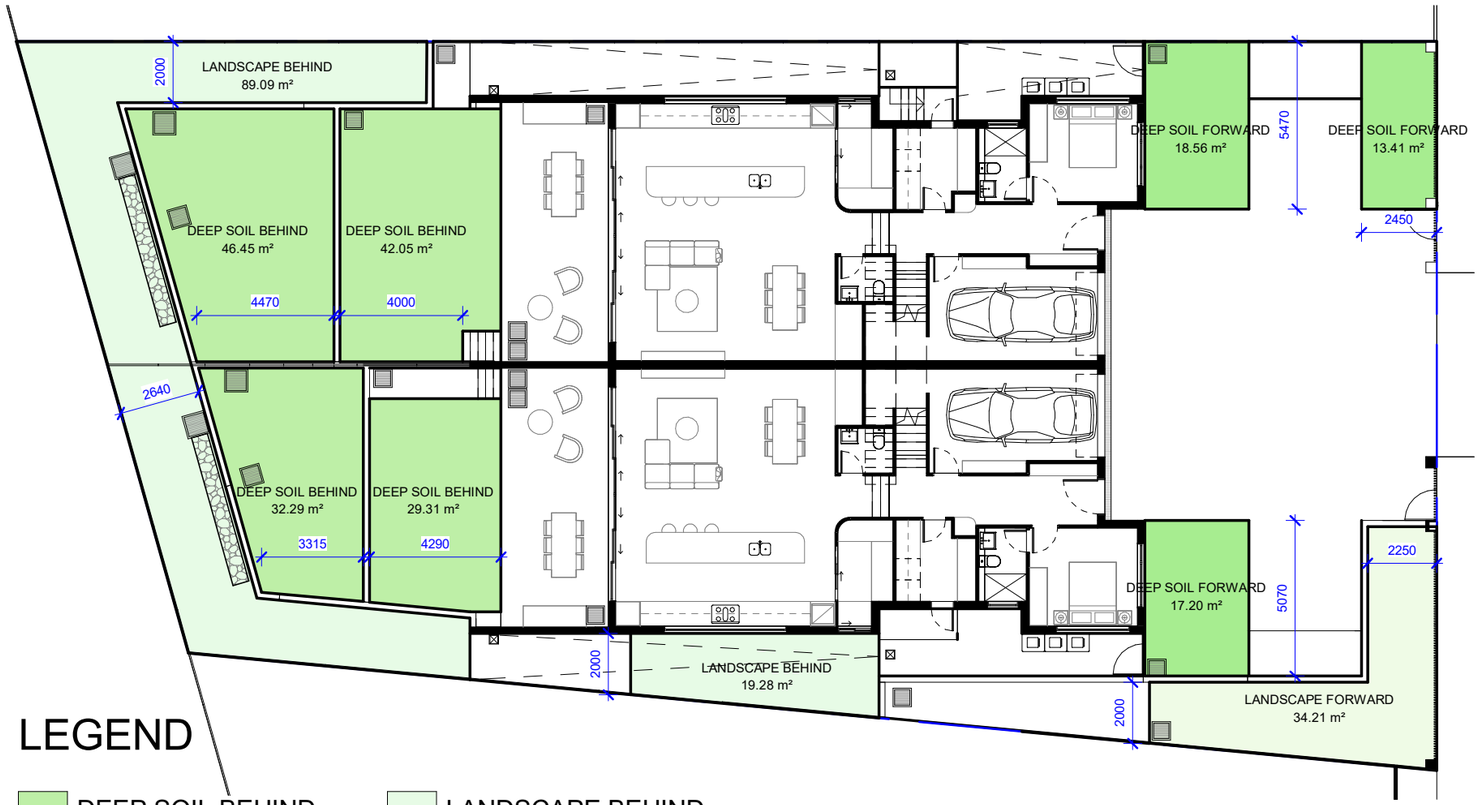

LEGEND

- DEEP SOIL BEHIND
- DEEP SOIL FORWARD
- LANDSCAPE BEHIND
- LANDSCAPE FORWARD

SITE DATA			
SITE AREA	942.20 m²		
ZONING	R2		
MAX GFA	471.10 m²		
PROPOSED AREA - LOT 1 (No. 257)		**PROPOSED AREA - LOT 2 (No. 257A)**	
GROUND FLOOR	113.71 m²	GROUND FLOOR	113.71 m²
LEVEL 1	121.79 m²	LEVEL 1	121.79 m²
TOTAL	235.50 m²	TOTAL	235.50 m²
TOTAL PROPOSED AREA			471.00 m²

COMPLIANCE TABLE		
CONTROL	REQUIRED	PROPOSED
SITE AREA	400.00 m²	942.20 m²
PRIMARY RD SETBACK	9.52 m	9.52 m
SIDE SETBACK - GF	0.90 m	0.90 m
SIDE SETBACK - L1	1.90 m	1.90 m
REAR SETBACK - GF	3.00 m	3.00 m
REAR SETBACK - L1	8.00 m	8.00 m
MIN LANDSCAPED AREA	376.88 m²	341.47 m²
- FORWARD OF THE BUILDING LINE	0.00 m²	83.38 m²
- BEHIND OF THE BUILDING LINE	188.44 m²	258.09 m²
MIN DEEP SOIL	282.66 m²	209.59 m²
- FORWARD OF THE BUILDING LINE	56.53 m²	49.17 m²
- BEHIND OF THE BUILDING LINE	141.33 m²	160.42 m²
NUMBER OF PARKING	1	2

NOTES

- ALL WORKS TO BE IN ACCORDANCE WITH THE BUILDING CODE OF AUSTRALIA, AUSTRALIAN STANDARDS, STATUTORY REGULATIONS AND LOCAL AUTHORITY REQUIREMENTS.
- CONTRACTOR TO ENSURE CONSISTENCY BETWEEN SIMILAR MATERIAL IS MAINTAINED.
- PREPARE & MAKE GOOD ALL SURFACES & SUBSTRATE AS REQUIRED TO RECEIVE NEW FINISHES AS PER MANUFACTURER'S SPECIFICATION.
- ALL DIMENSIONS TO BE CHECKED ON SITE BEFORE COMMENCEMENT OF WORK. ALL DIMENSIONS MUST BE CHECKED & VERIFIED ON SITE PRIOR TO CONSTRUCTION & MANUFACTURE OF ANY ITEM.
- THIS DRAWING IS COPYRIGHT AND THE PROPERTY OF THE AUTHOR. IT MUST NOT BE RETAINED, COPIED OR USED WITHOUT THE EXPRESS AUTHORITY OF PLAY CO PTY LTD.

REV	DATE	DESCRIPTION
P1	19/09/25	PRELIMINARY PLAN
P2	08/12/25	PRELIMINARY PLAN
P3	21/01/26	PRELIMINARY PLAN
A	17/02/26	DA SUBMISSION
B	10/07/26	RFI
C	29/07/26	RFI

PROJECT

257 MARSDEN ROAD CARLINGFORD


ARCHITECT

PLAY CO PTY LTD

ABN 206 135 521 86
SUITE 801, 11 HELP STREET
CHATSWOOD NSW 2067
WWW.PLAY-CO.COM.AU
NOMINATED ARCHITECT
RAYMOND NG #8961
DESIGN PRACTITIONER DEP000234


CLIENT

PROJECT NUMBER	P632	PROJECT ADDRESS	257 MARSDEN ROAD CARLINGFORD		
DRAWING NUMBER	A501	DRAWING TITLE	LANDSCAPE DIAGRAM		
SCALE	1 : 200	PAPER SIZE	A3	REVISION	C
DRAWN BY	TT	REVIEWED BY	RN	STATUS	RFI

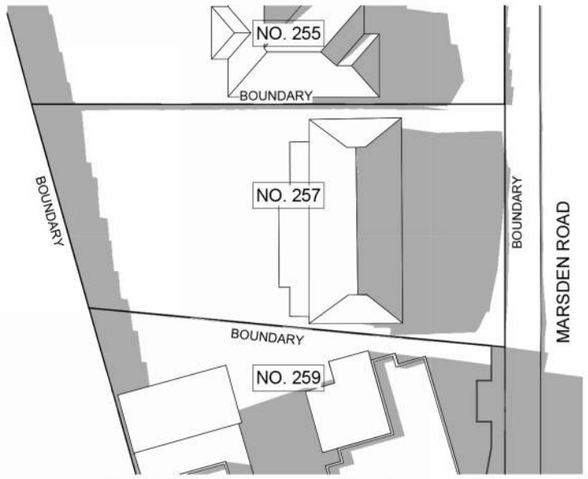


1 EXISTING 21 JUNE - 9AM

1 : 600

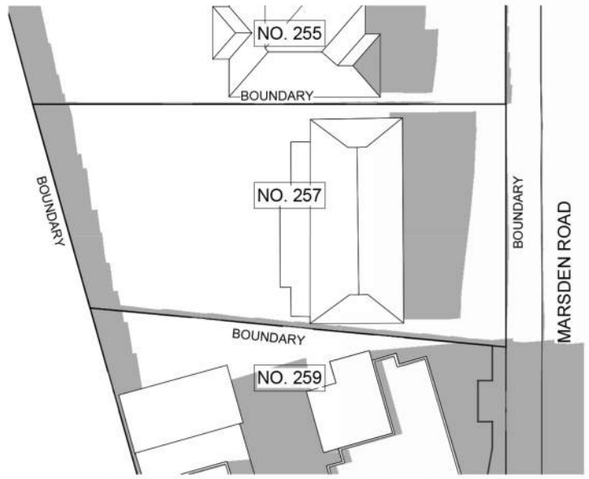


2 EXISTING 21 JUNE - 10AM

1 : 600

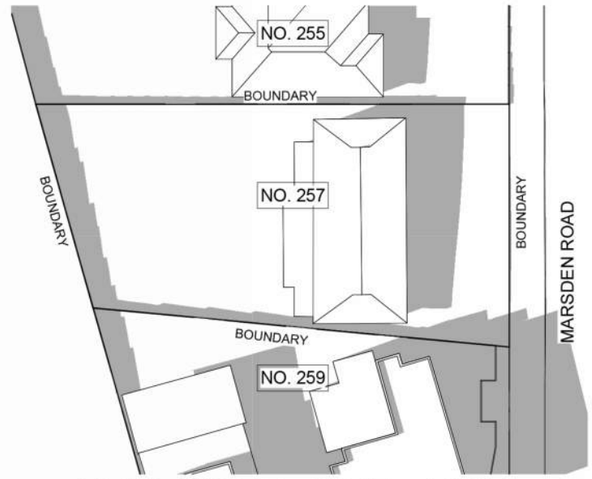


3 EXISTING 21 JUNE - 11AM

1 : 600

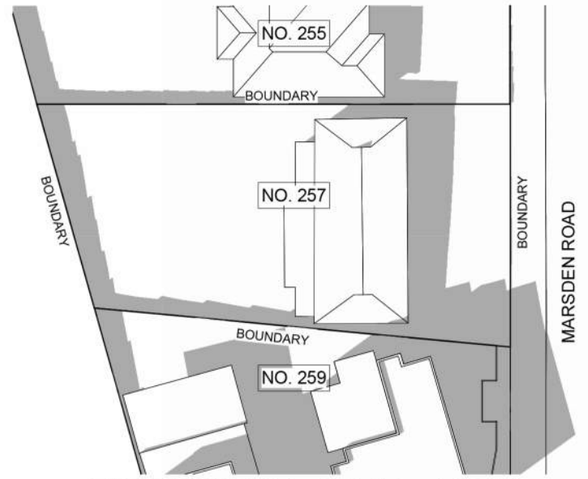


4 EXISTING 21 JUNE - 12PM

1 : 600

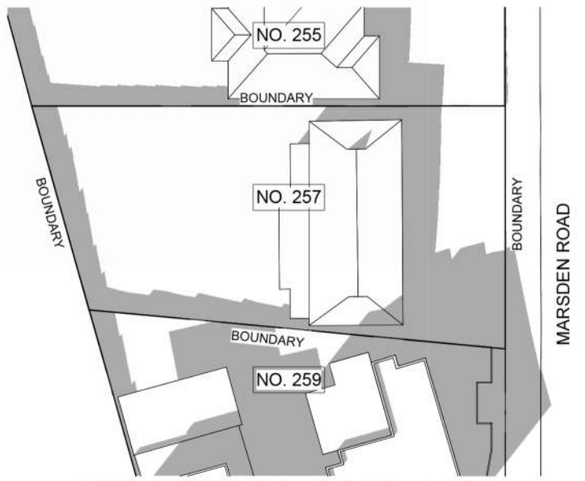


5 EXISTING 21 JUNE - 1PM

1 : 600

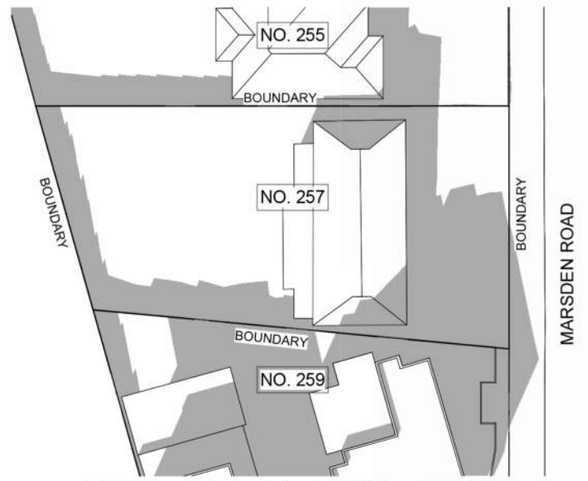

6 EXISTING 21 JUNE - 2PM

1 : 600

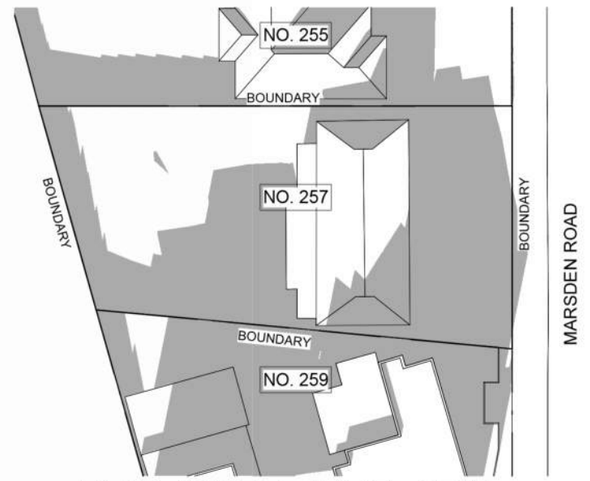

7 EXISTING 21 JUNE - 3PM

1 : 600

LEGEND

- EXISTING SHADOWS
- ADDITION SHADOW CAST BY PROPOSED DEVELOPMENT COMPARED TO EXISTING BUILDING
- REDUCED SHADOW CAST BY PROPOSED DEVELOPMENT COMPARED TO EXISTING BUILDING

NOTES

- ALL WORKS TO BE IN ACCORDANCE WITH THE BUILDING CODE OF AUSTRALIA, AUSTRALIAN STANDARDS, STATUTORY REGULATIONS AND LOCAL AUTHORITY REQUIREMENTS.
- CONTRACTOR TO ENSURE CONSISTENCY BETWEEN SIMILAR MATERIAL IS MAINTAINED.
- PREPARE & MAKE GOOD ALL SURFACES & SUBSTRATE AS REQUIRED TO RECEIVE NEW FINISHES AS PER MANUFACTURER'S SPECIFICATION.
- ALL DIMENSIONS TO BE CHECKED ON SITE BEFORE COMMENCEMENT OF WORK. ALL DIMENSIONS MUST BE CHECKED & VERIFIED ON SITE PRIOR TO CONSTRUCTION & MANUFACTURE OF ANY ITEM.
- THIS DRAWING IS COPYRIGHT AND THE PROPERTY OF THE AUTHOR. IT MUST NOT BE RETAINED, COPIED OR USED WITHOUT THE EXPRESS AUTHORITY OF PLAY CO PTY LTD.

REV	DATE	DESCRIPTION
P1	19/09/25	PRELIMINARY PLAN
P2	08/12/25	PRELIMINARY PLAN
P3	21/01/26	PRELIMINARY PLAN
A	17/02/26	DA SUBMISSION
B	10/07/26	RFI
C	29/07/26	RFI

PROJECT


257 MARSDEN ROAD CARLINGFORD

ARCHITECT

PLAY CO ARCHITECTS
PLAY CO PTY LTD
ABN 206 135 521 86
SUITE 801, 11 HELP STREET
CHATSWOOD NSW 2067
WWW.PLAY-CO.COM.AU
NOMINATED ARCHITECT
RAYMOND NG #8961
DESIGN PRACTITIONER DEP000234


CLIENT

PROJECT NUMBER	P632	PROJECT ADDRESS	257 MARSDEN ROAD CARLINGFORD		
DRAWING NUMBER	A502	DRAWING TITLE	EXISTING SHADOW DIAGRAM		
SCALE	1 : 600	PAPER SIZE	A3	REVISION	C
DRAWN BY	TT	REVIEWED BY	RN	STATUS	RFI

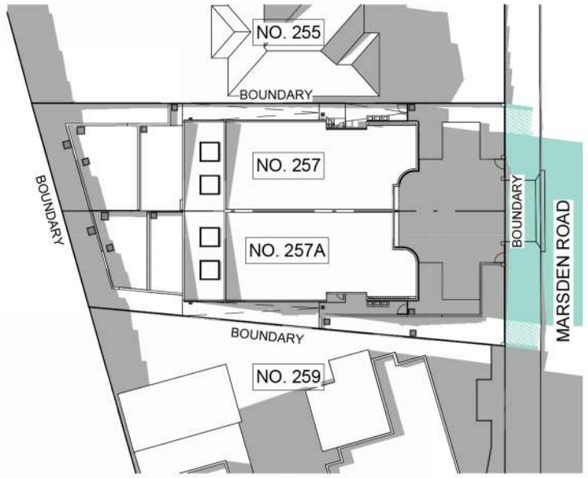


1 PROPOSED 21 JUNE - 9AM

1 : 600

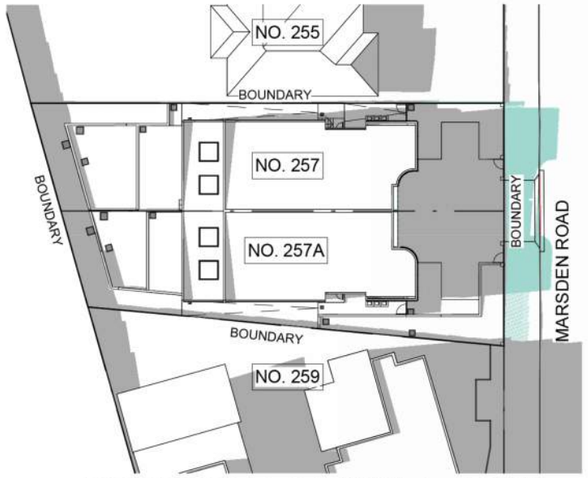

2 PROPOSED 21 JUNE - 10AM

1 : 600

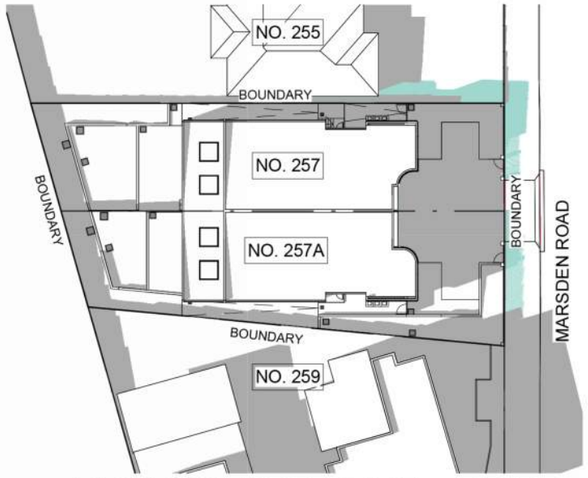


3 PROPOSED 21 JUNE - 11AM

1 : 600




4 PROPOSED 21 JUNE - 12PM

1 : 600

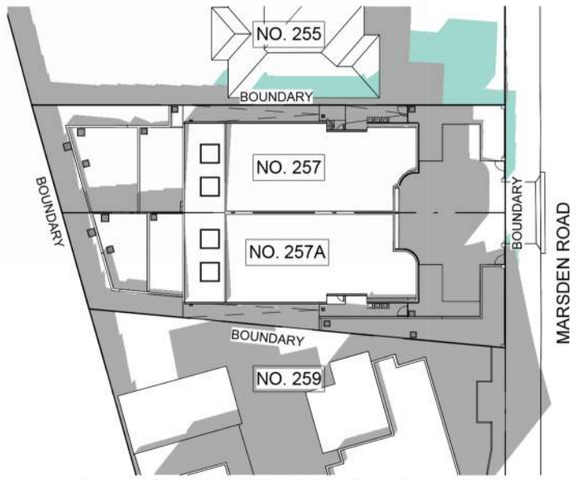


5 PROPOSED 21 JUNE - 1PM

1 : 600

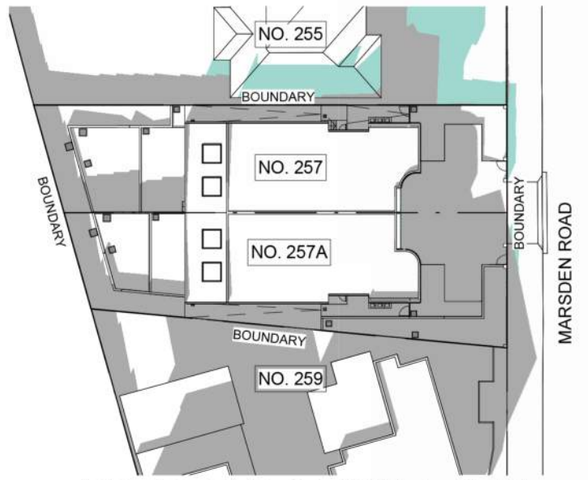

6 PROPOSED 21 JUNE - 2PM

1 : 600

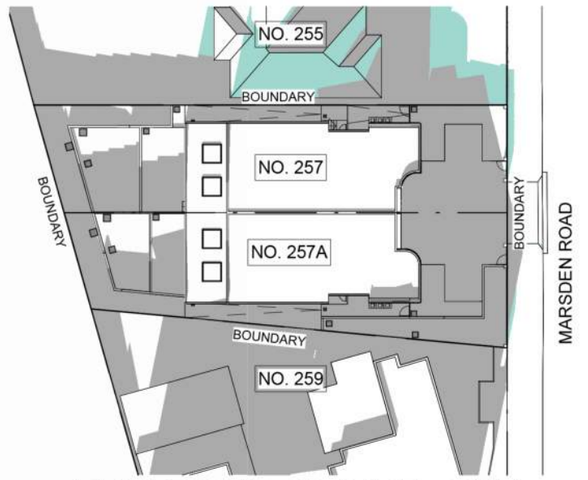

7 PROPOSED 21 JUNE - 3PM

1 : 600

LEGEND

- EXISTING SHADOWS
- ADDITION SHADOW CAST BY PROPOSED DEVELOPMENT COMPARED TO EXISTING BUILDING
- REDUCED SHADOW CAST BY PROPOSED DEVELOPMENT COMPARED TO EXISTING BUILDING

NOTES

- ALL WORKS TO BE IN ACCORDANCE WITH THE BUILDING CODE OF AUSTRALIA, AUSTRALIAN STANDARDS, STATUTORY REGULATIONS AND LOCAL AUTHORITY REQUIREMENTS.
- CONTRACTOR TO ENSURE CONSISTENCY BETWEEN SIMILAR MATERIAL IS MAINTAINED.
- PREPARE & MAKE GOOD ALL SURFACES & SUBSTRATE AS REQUIRED TO RECEIVE NEW FINISHES AS PER MANUFACTURER'S SPECIFICATION.
- ALL DIMENSIONS TO BE CHECKED ON SITE BEFORE COMMENCEMENT OF WORK. ALL DIMENSIONS MUST BE CHECKED & VERIFIED ON SITE PRIOR TO CONSTRUCTION & MANUFACTURE OF ANY ITEM.
- THIS DRAWING IS COPYRIGHT AND THE PROPERTY OF THE AUTHOR. IT MUST NOT BE RETAINED, COPIED OR USED WITHOUT THE EXPRESS AUTHORITY OF PLAY CO PTY LTD.

REV	DATE	DESCRIPTION
P1	19/09/25	PRELIMINARY PLAN
P2	08/12/25	PRELIMINARY PLAN
P3	21/01/26	PRELIMINARY PLAN
A	17/02/26	DA SUBMISSION
B	10/07/26	RFI
C	29/07/26	RFI

PROJECT

257 MARSDEN ROAD CARLINGFORD

ARCHITECT


PLAY CO ARCHITECTS

PLAY CO PTY LTD


ABN 206 135 521 86
SUITE 801, 11 HELP STREET
CHATSWOOD NSW 2067
WWW.PLAY-CO.COM.AU
NOMINATED ARCHITECT
RAYMOND NG #8961
DESIGN PRACTITIONER DEP000234

CLIENT


PROJECT NUMBER	P632	PROJECT ADDRESS	257 MARSDEN ROAD CARLINGFORD
DRAWING NUMBER	A503	DRAWING TITLE	PROPOSED SHADOW DIAGRAM
SCALE	1 : 600	PAPER SIZE	A3
DRAWN BY	TT	REVIEWED BY	RN
		REVISION	C
		STATUS	RFI

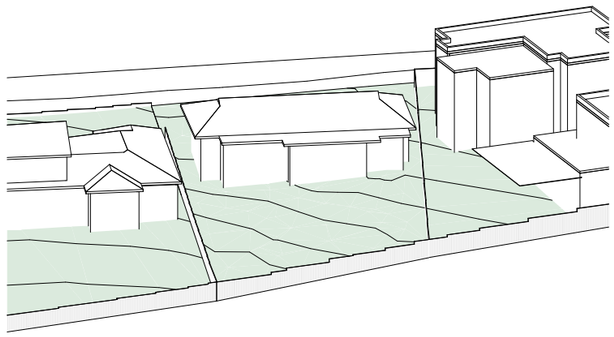


1 EXISTING 21 JUNE - 9AM

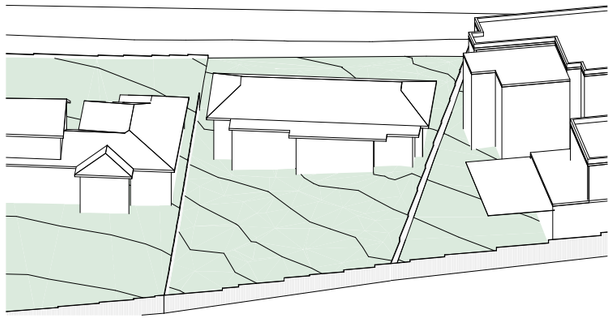


2 EXISTING 21 JUNE - 10AM

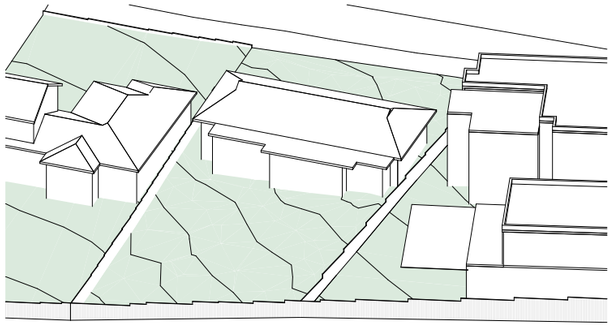


3 EXISTING 21 JUNE - 11AM

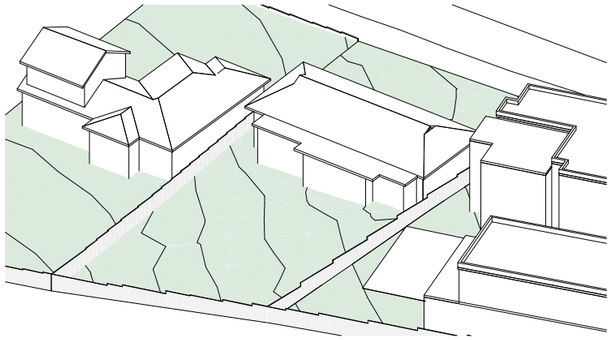


4 EXISTING 21 JUNE - 12PM

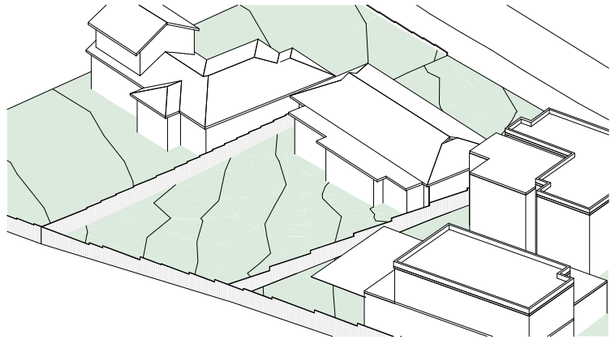

5 EXISTING 21 JUNE - 1PM

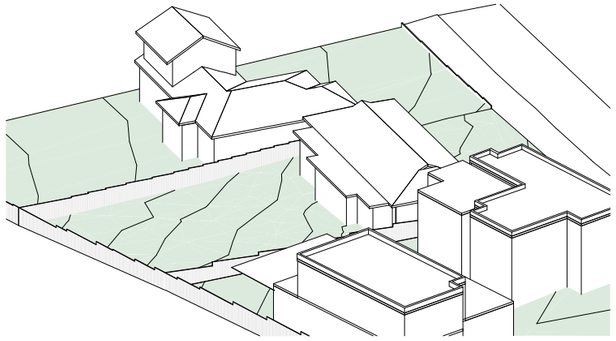

6 EXISTING 21 JUNE - 2PM

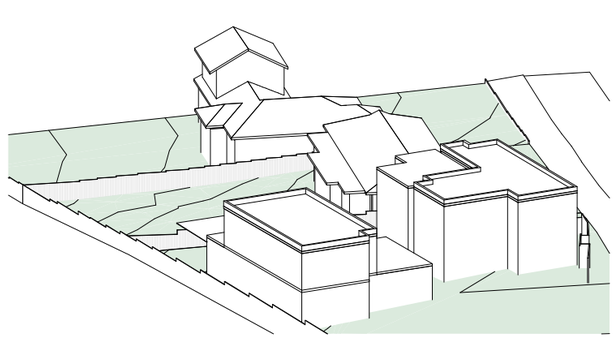

7 EXISTING 21 JUNE - 3PM

NOTES

- ALL WORKS TO BE IN ACCORDANCE WITH THE BUILDING CODE OF AUSTRALIA, AUSTRALIAN STANDARDS, STATUTORY REGULATIONS AND LOCAL AUTHORITY REQUIREMENTS.
- CONTRACTOR TO ENSURE CONSISTENCY BETWEEN SIMILAR MATERIAL IS MAINTAINED.
- PREPARE & MAKE GOOD ALL SURFACES & SUBSTRATE AS REQUIRED TO RECEIVE NEW FINISHES AS PER MANUFACTURER'S SPECIFICATION.
- ALL DIMENSIONS TO BE CHECKED ON SITE BEFORE COMMENCEMENT OF WORK. ALL DIMENSIONS MUST BE CHECKED & VERIFIED ON SITE PRIOR TO CONSTRUCTION & MANUFACTURE OF ANY ITEM.
- THIS DRAWING IS COPYRIGHT AND THE PROPERTY OF THE AUTHOR. IT MUST NOT BE RETAINED, COPIED OR USED WITHOUT THE EXPRESS AUTHORITY OF PLAY CO PTY LTD.

REV	DATE	DESCRIPTION
P1	19/09/25	PRELIMINARY PLAN
P2	08/12/25	PRELIMINARY PLAN
P3	21/01/26	PRELIMINARY PLAN
A	17/02/26	DA SUBMISSION
B	10/07/26	RFI
C	29/07/26	RFI

PROJECT
257 MARSDEN ROAD CARLINGFORD

ARCHITECT


PLAY CO ARCHITECTS
ARCHITECTURE | INTERIORS | PROJECT MANAGEMENT
PLAY CO PTY LTD

ABN 206 135 521 86
SUITE 801, 11 HELP STREET
CHATSWOOD NSW 2067
WWW.PLAY-CO.COM.AU
NOMINATED ARCHITECT
RAYMOND NG #8961
DESIGN PRACTITIONER DEP000234


CLIENT

PROJECT NUMBER	P632	PROJECT ADDRESS	257 MARSDEN ROAD CARLINGFORD
DRAWING NUMBER	A510	DRAWING TITLE	EXISTING SOLAR DIAGRAM


SCALE		PAPER SIZE	A3	REVISION	C
DRAWN BY	TT	REVIEWED BY	RN	STATUS	RFI

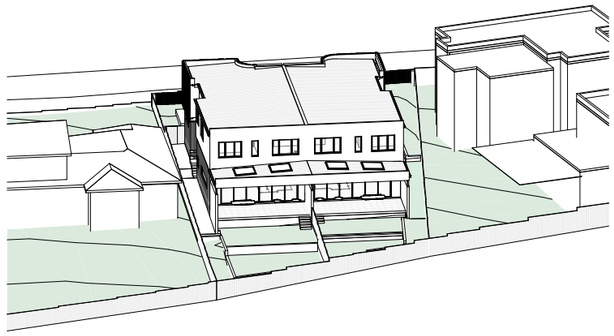


1 PROPOSED 21 JUNE - 9AM

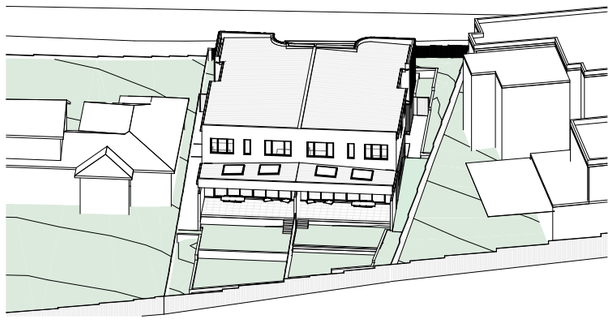


2 PROPOSED 21 JUNE - 10AM

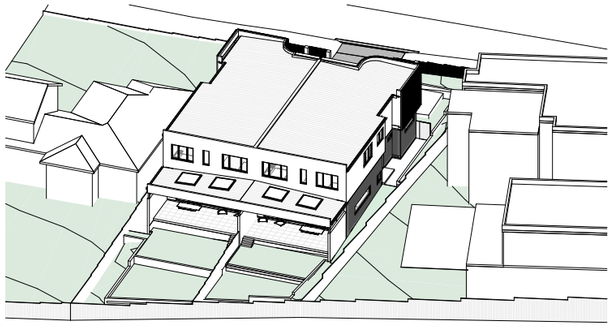


3 PROPOSED 21 JUNE - 11AM

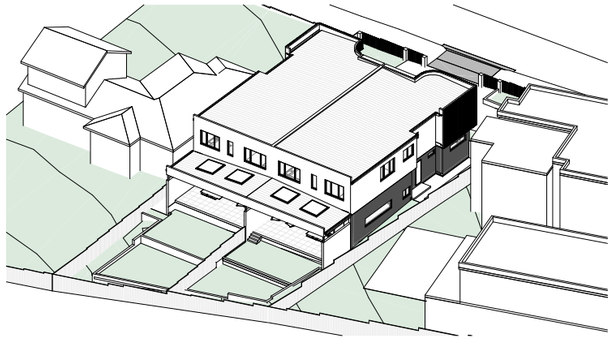


4 PROPOSED 21 JUNE - 12PM

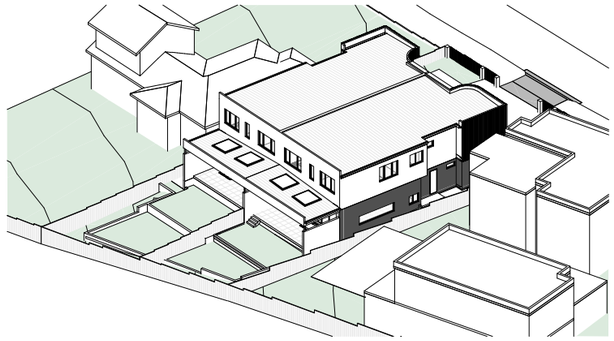

5 PROPOSED 21 JUNE - 1PM

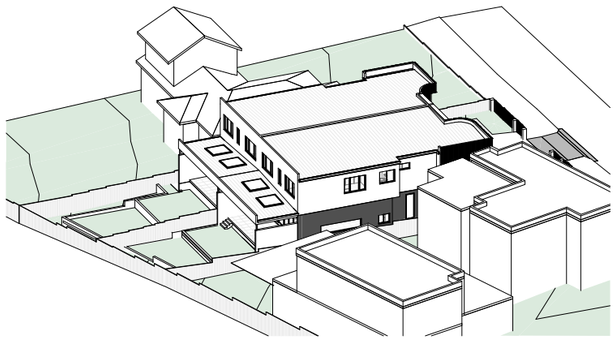

6 PROPOSED 21 JUNE - 2PM

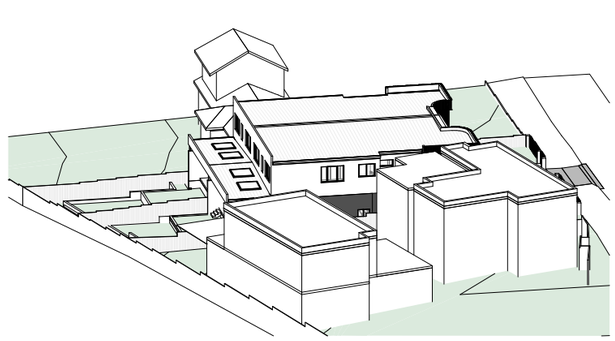

7 PROPOSED 21 JUNE - 3PM

NOTES

- ALL WORKS TO BE IN ACCORDANCE WITH THE BUILDING CODE OF AUSTRALIA, AUSTRALIAN STANDARDS, STATUTORY REGULATIONS AND LOCAL AUTHORITY REQUIREMENTS.
- CONTRACTOR TO ENSURE CONSISTENCY BETWEEN SIMILAR MATERIAL IS MAINTAINED.
- PREPARE & MAKE GOOD ALL SURFACES & SUBSTRATE AS REQUIRED TO RECEIVE NEW FINISHES AS PER MANUFACTURER'S SPECIFICATION.
- ALL DIMENSIONS TO BE CHECKED ON SITE BEFORE COMMENCEMENT OF WORK. ALL DIMENSIONS MUST BE CHECKED & VERIFIED ON SITE PRIOR TO CONSTRUCTION & MANUFACTURE OF ANY ITEM.
- THIS DRAWING IS COPYRIGHT AND THE PROPERTY OF THE AUTHOR. IT MUST NOT BE RETAINED, COPIED OR USED WITHOUT THE EXPRESS AUTHORITY OF PLAY CO PTY LTD.

REV	DATE	DESCRIPTION
P1	19/09/25	PRELIMINARY PLAN
P2	08/12/25	PRELIMINARY PLAN
P3	21/01/26	PRELIMINARY PLAN
A	17/02/26	DA SUBMISSION
B	10/07/26	RFI
C	29/07/26	RFI

PROJECT

257 MARSDEN ROAD CARLINGFORD

ARCHITECT

PLAY CO ARCHITECTS
ARCHITECTURE | INTERIORS | PROJECT MANAGEMENT
PLAY CO PTY LTD
ABN 206 135 521 86
SUITE 801, 11 HELP STREET
CHATSWOOD NSW 2067
WWW.PLAY-CO.COM.AU
NOMINATED ARCHITECT
RAYMOND NG #8961
DESIGN PRACTITIONER DEP000234

CLIENT

PROJECT NUMBER	P632	PROJECT ADDRESS	257 MARSDEN ROAD CARLINGFORD
DRAWING NUMBER	A511	DRAWING TITLE	PROPOSED SOLAR DIAGRAM

SCALE		PAPER SIZE	A3	REVISION	C
DRAWN BY	TT	REVIEWED BY	RN	STATUS	RFI



NOTES

- ALL WORKS TO BE IN ACCORDANCE WITH THE BUILDING CODE OF AUSTRALIA, AUSTRALIAN STANDARDS, STATUTORY REGULATIONS AND LOCAL AUTHORITY REQUIREMENTS.
- CONTRACTOR TO ENSURE CONSISTENCY BETWEEN SIMILAR MATERIAL IS MAINTAINED.
- PREPARE & MAKE GOOD ALL SURFACES & SUBSTRATE AS REQUIRED TO RECEIVE NEW FINISHES AS PER MANUFACTURER'S SPECIFICATION.
- ALL DIMENSIONS TO BE CHECKED ON SITE BEFORE COMMENCEMENT OF WORK. ALL DIMENSIONS MUST BE CHECKED & VERIFIED ON SITE PRIOR TO CONSTRUCTION & MANUFACTURE OF ANY ITEM.
- THIS DRAWING IS COPYRIGHT AND THE PROPERTY OF THE AUTHOR. IT MUST NOT BE RETAINED, COPIED OR USED WITHOUT THE EXPRESS AUTHORITY OF PLAY CO PTY LTD.

REV	DATE	DESCRIPTION
P1	19/09/25	PRELIMINARY PLAN
P2	08/12/25	PRELIMINARY PLAN
P3	21/01/26	PRELIMINARY PLAN
A	17/02/26	DA SUBMISSION
B	10/07/26	RFI
C	29/07/26	RFI

PROJECT

257 MARSDEN ROAD CARLINGFORD

ARCHITECT

PLAY CO ARCHITECTS
ARCHITECTURE | INTERIORS | PROJECT MANAGEMENT
PLAY CO PTY LTD

ABN 206 135 521 86
SUITE 801, 11 HELP STREET
CHATSWOOD NSW 2067
WWW.PLAY-CO.COM.AU
NOMINATED ARCHITECT
RAYMOND NG #8961
DESIGN PRACTITIONER DEP000234

CLIENT

PROJECT NUMBER	P632	PROJECT ADDRESS	257 MARSDEN ROAD CARLINGFORD
DRAWING NUMBER	A602	DRAWING TITLE	PROPOSED PERSPECTIVE

SCALE		PAPER SIZE	A3	REVISION	C
DRAWN BY	TT	REVIEWED BY	RN	STATUS	RFI







NOTES

- ALL WORKS TO BE IN ACCORDANCE WITH THE BUILDING CODE OF AUSTRALIA, AUSTRALIAN STANDARDS, STATUTORY REGULATIONS AND LOCAL AUTHORITY REQUIREMENTS.
- CONTRACTOR TO ENSURE CONSISTENCY BETWEEN SIMILAR MATERIAL IS MAINTAINED.
- PREPARE & MAKE GOOD ALL SURFACES & SUBSTRATE AS REQUIRED TO RECEIVE NEW FINISHES AS PER MANUFACTURER'S SPECIFICATION.
- ALL DIMENSIONS TO BE CHECKED ON SITE BEFORE COMMENCEMENT OF WORK. ALL DIMENSIONS MUST BE CHECKED & VERIFIED ON SITE PRIOR TO CONSTRUCTION & MANUFACTURE OF ANY ITEM.
- THIS DRAWING IS COPYRIGHT AND THE PROPERTY OF THE AUTHOR. IT MUST NOT BE RETAINED, COPIED OR USED WITHOUT THE EXPRESS AUTHORITY OF PLAY CO PTY LTD.

REV	DATE	DESCRIPTION
P1	19/09/25	PRELIMINARY PLAN
P2	08/12/25	PRELIMINARY PLAN
P3	21/01/26	PRELIMINARY PLAN
A	17/02/26	DA SUBMISSION
B	10/07/26	RFI
C	29/07/26	RFI

PROJECT

257 MARSDEN ROAD CARLINGFORD

ARCHITECT

PLAY CO PTY LTD

ABN 206 135 521 86
SUITE 801, 11 HELP STREET
CHATSWOOD NSW 2067
WWW.PLAY-CO.COM.AU
NOMINATED ARCHITECT
RAYMOND NG #8961
DESIGN PRACTITIONER DEP000234

CLIENT

PROJECT NUMBER	P632	PROJECT ADDRESS	257 MARSDEN ROAD CARLINGFORD
DRAWING NUMBER	A603	DRAWING TITLE	PROPOSED PERSPECTIVE 2

SCALE		PAPER SIZE	A3	REVISION	C
DRAWN BY	TT	REVIEWED BY	RN	STATUS	RFI