



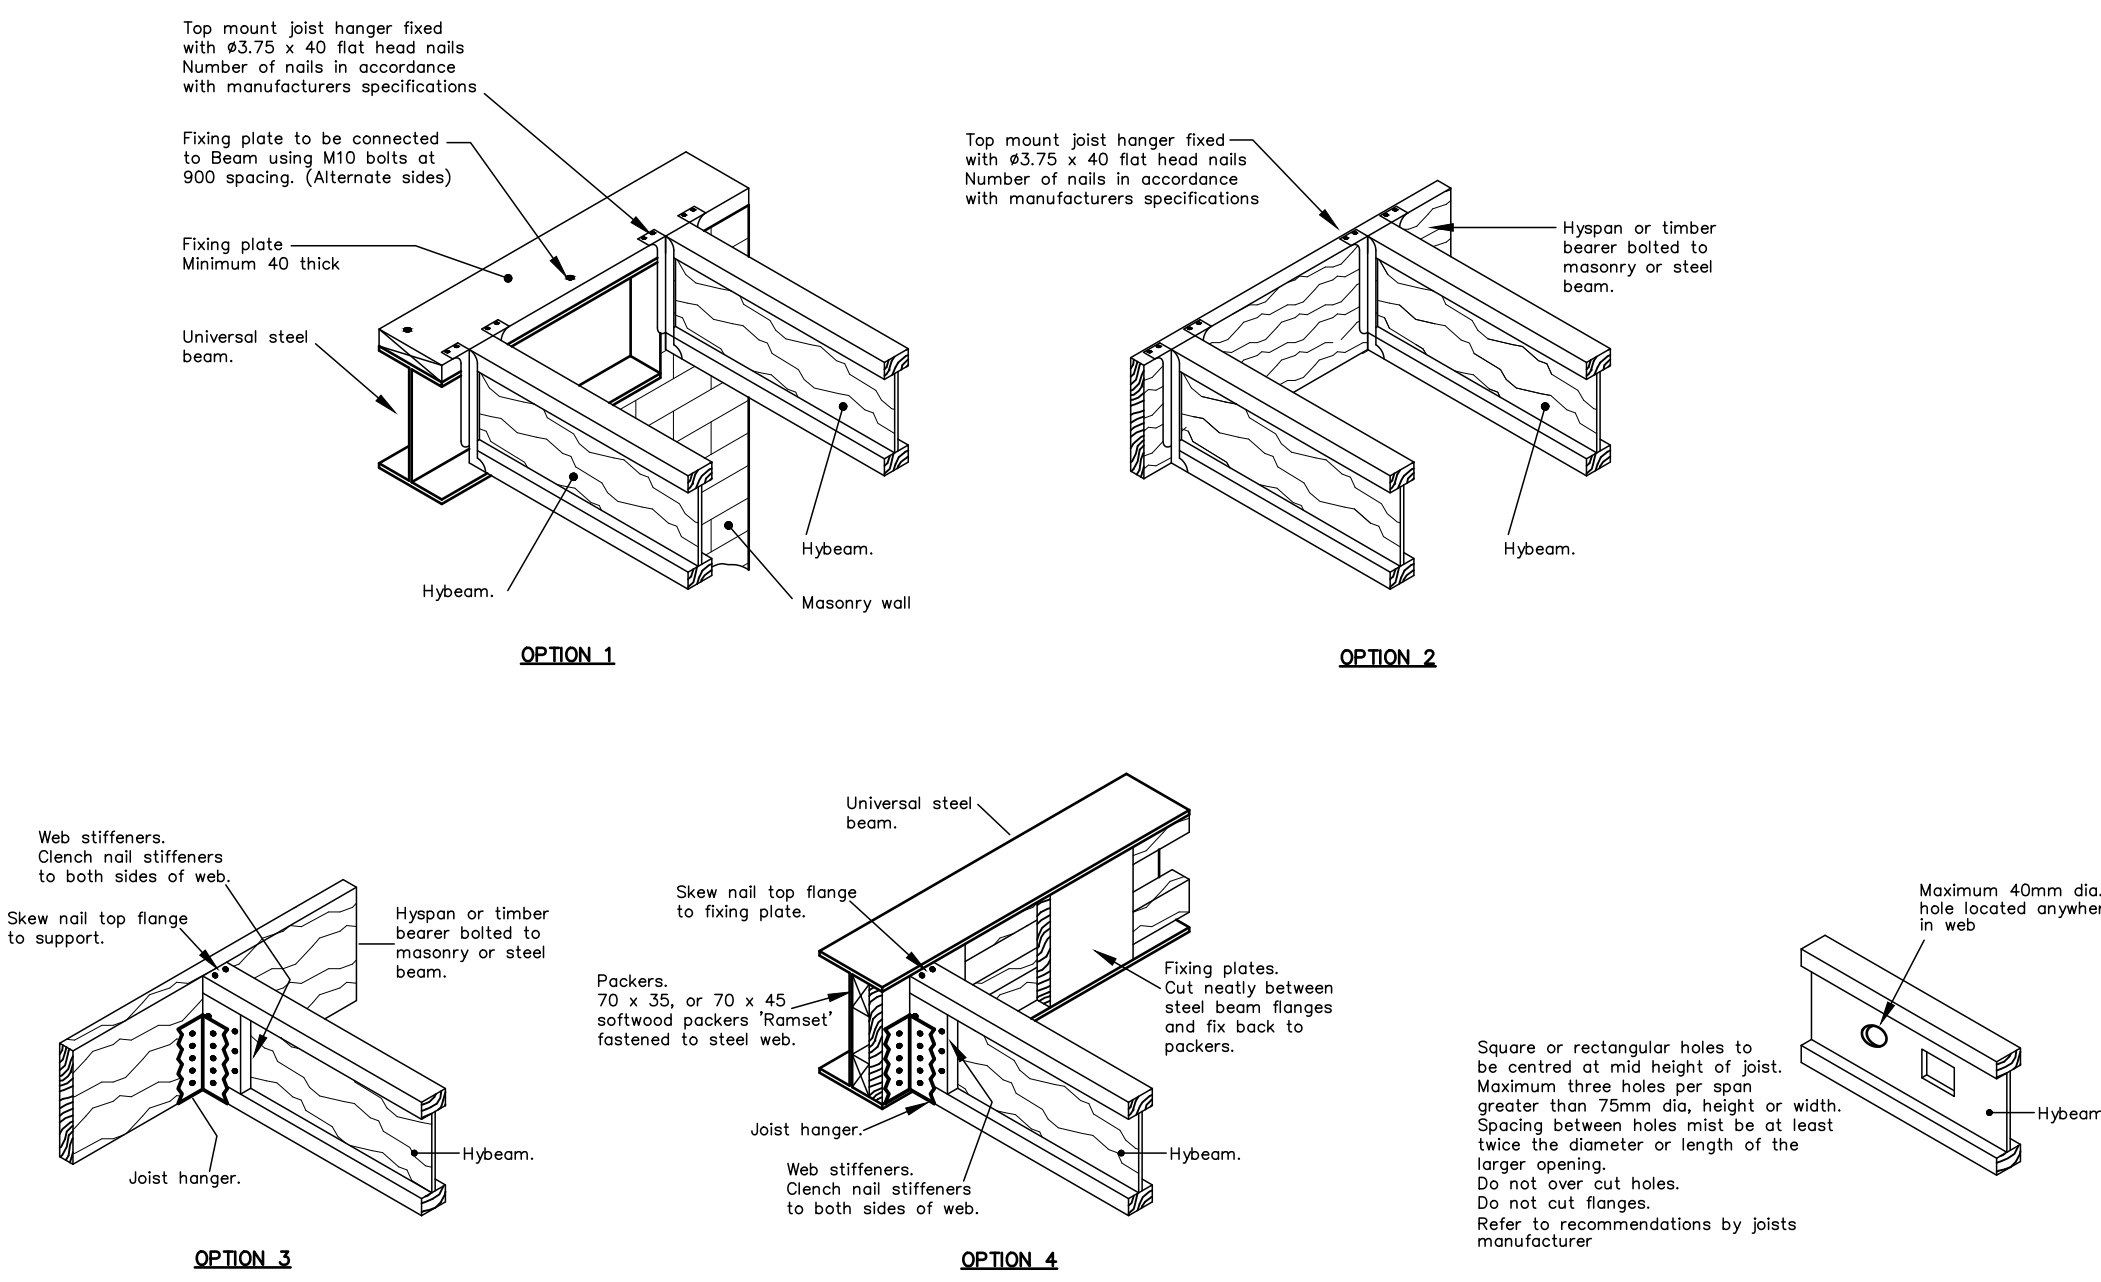

HYSPAN CONNECTION DETAILS


WEB HOLES FOR HYSPAN FLOOR JOISTS

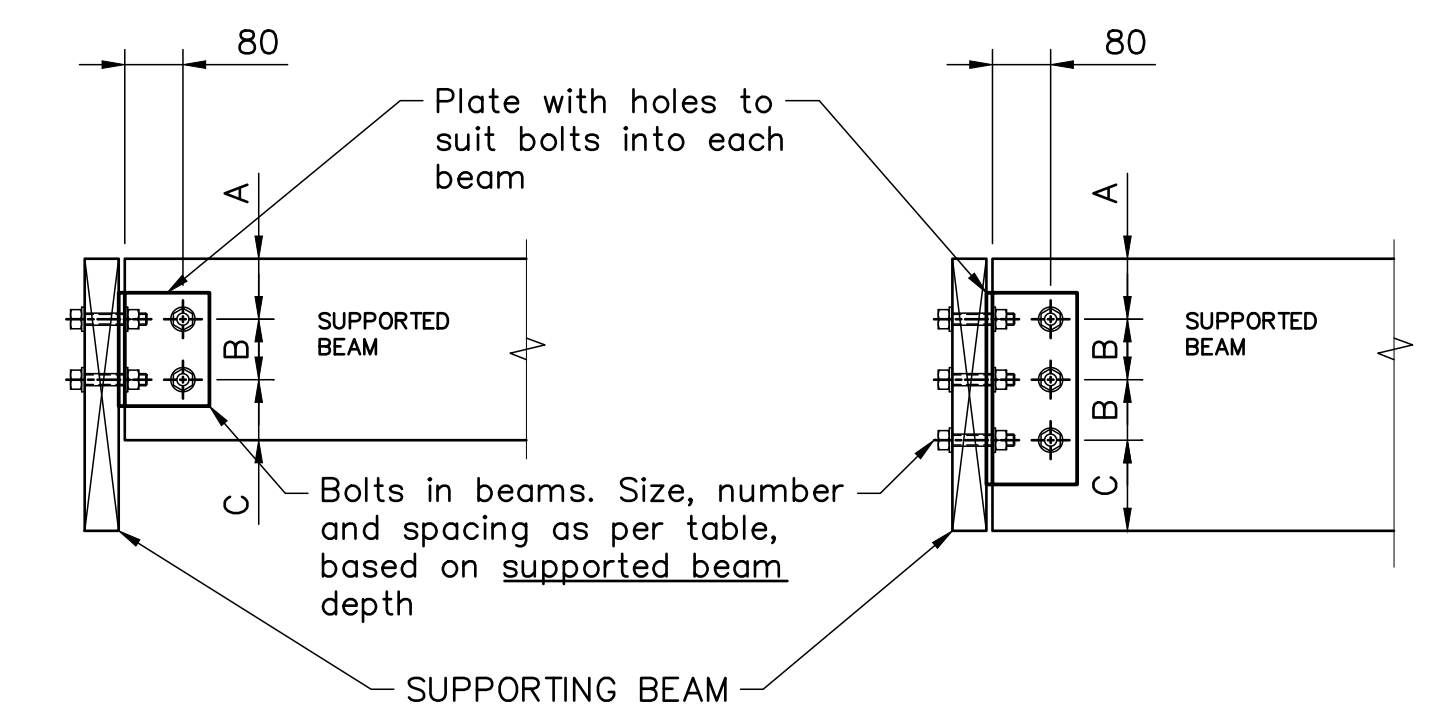


TIMBER BEAM CONNECTION (1:10)

Supported Beam Depth	Bolt Size	No. Bolts	Distance (min)			Plate Thickness
			A	B	C	
170	M12	2	50	60	50	6
190						
200	M16	2	65	80	55	8
240			65	80	65	8
290	M16	3	65	80	65	8
300						
360	M16	4	65	80	55	8


NOTE: Supporting beam is to be AT LEAST the depth and width of the supported beam

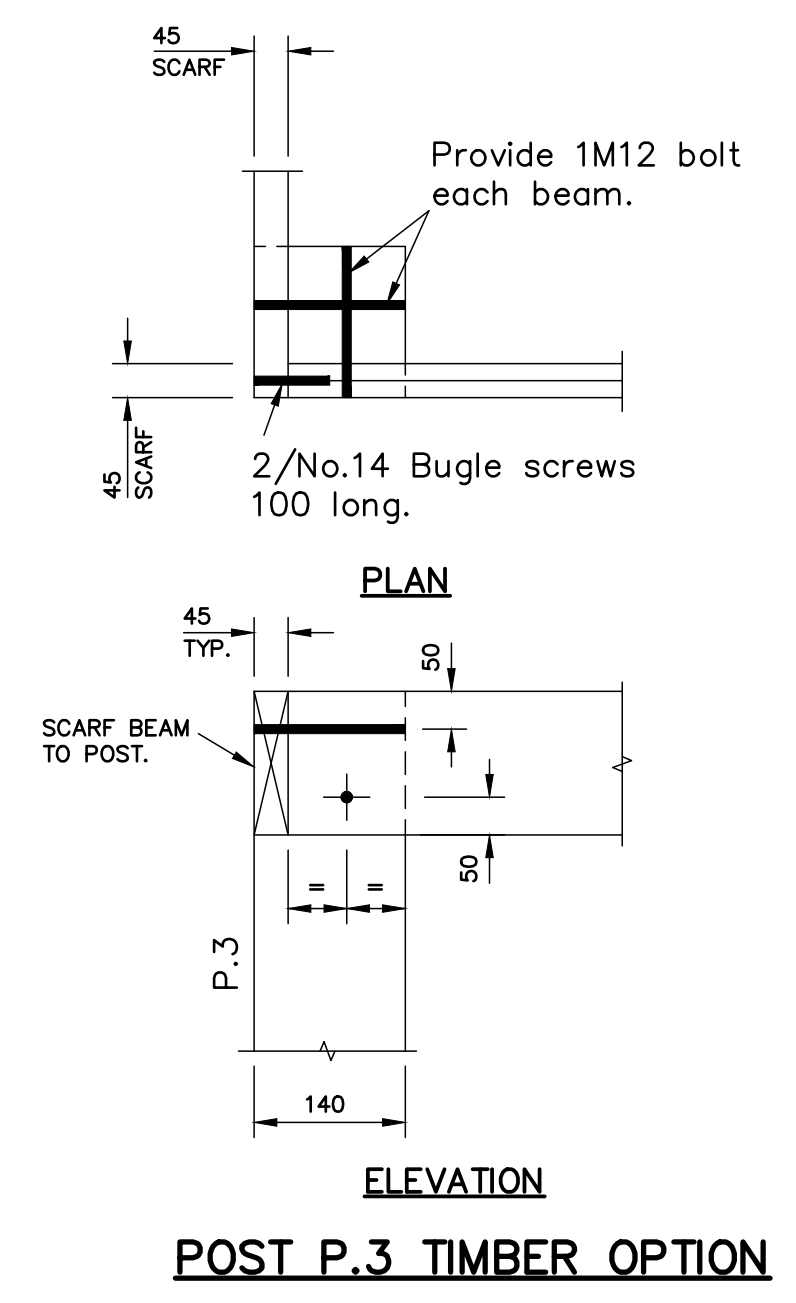


TYPICAL STEEL BEAM CONNECTION (1:10)

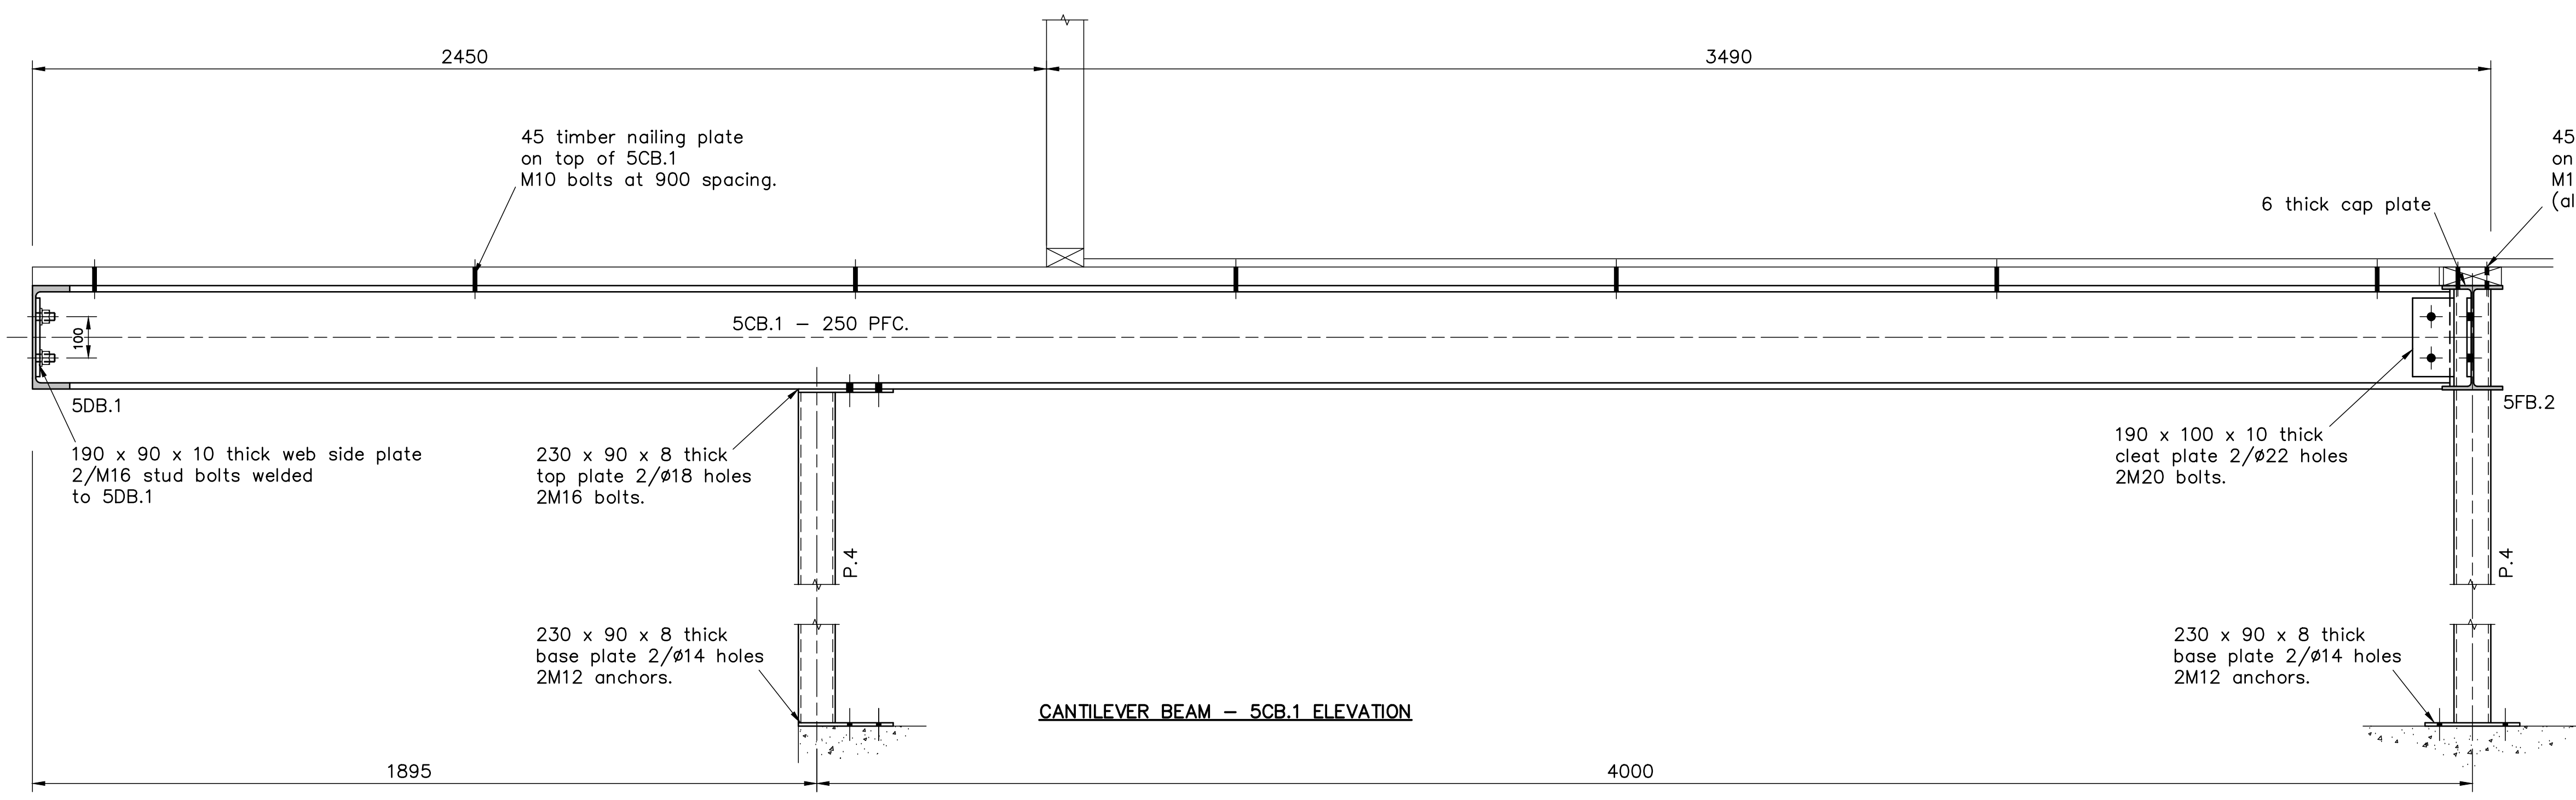


CANTILEVER BEAM - 5CB.1 ELEVATION

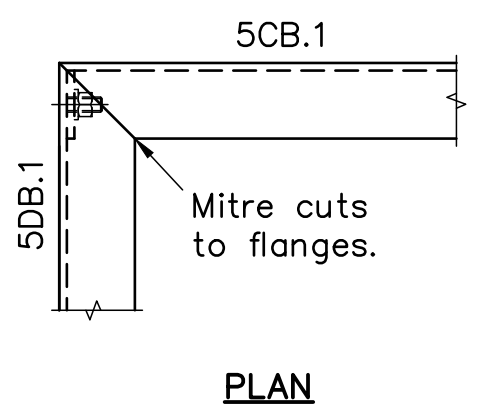


CANTILEVER BEAM - 5CB.1 DETAIL (1:10)

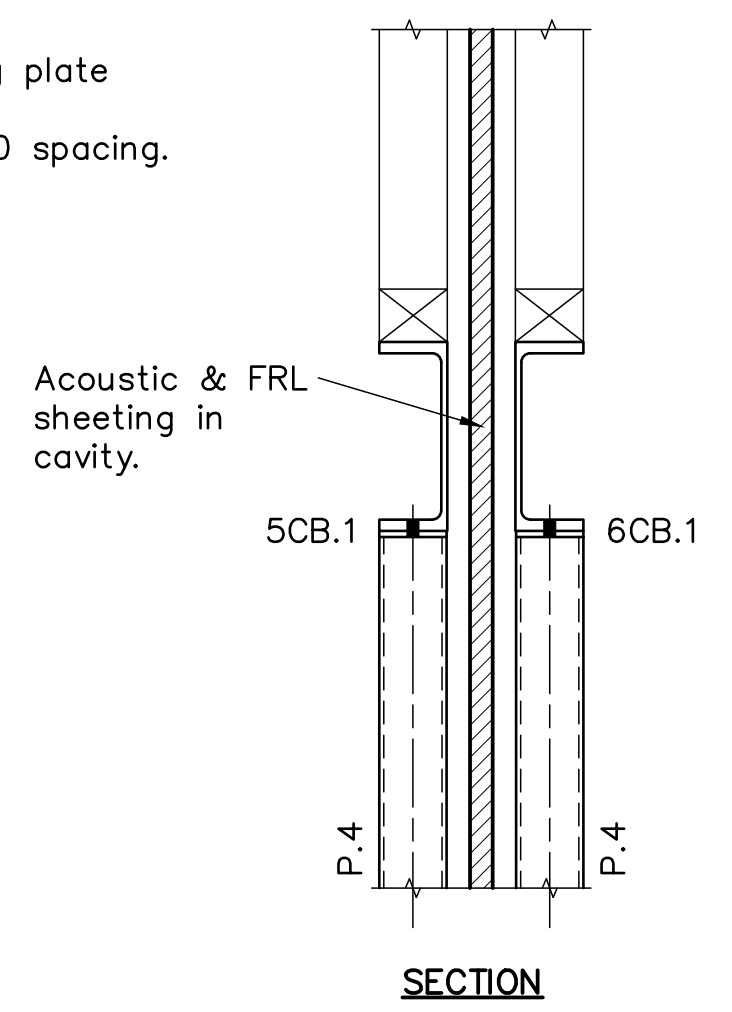

SECTION

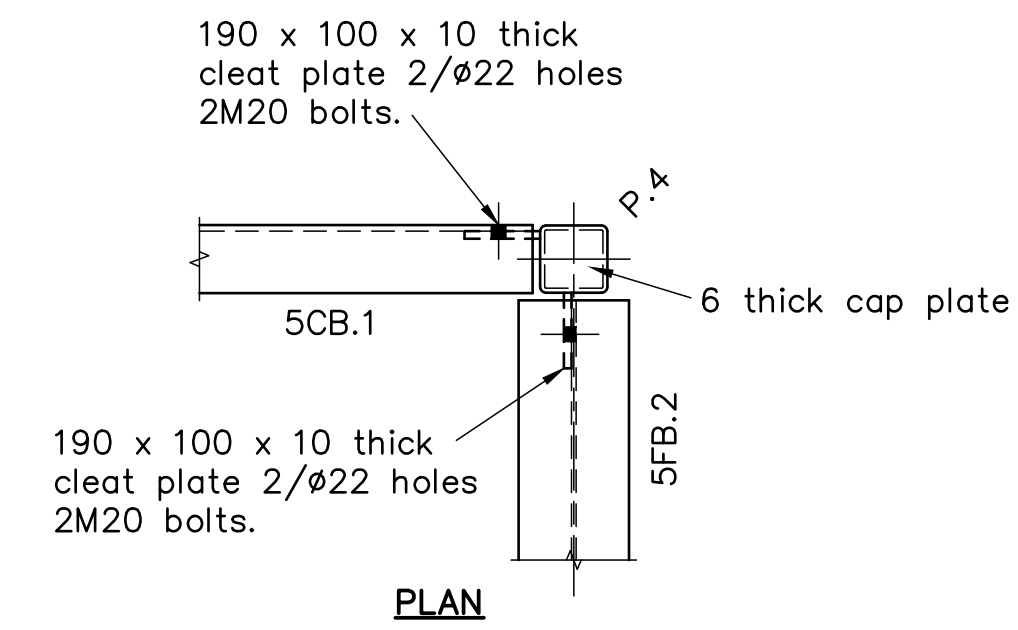

PLAN

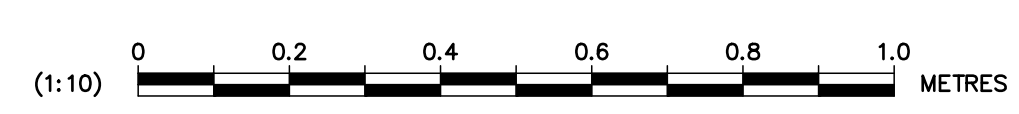

CAD FILE: 240601057

ORIGINAL SIZE - A1

ISSUE	DATE	DETAILS OF AMENDMENT

HALCROW & ASSOCIATES
CONSULTING STRUCTURAL ENGINEERS
A.C.N. 003 805 374
108 Avoca Drive,
Kincumber, N.S.W. 2251.
P.O. Box 6349 Kincumber, 2251
Phone: (02) 4369-0977
Email: design@halcrow.com.au

DESIGN: H.M.H.	DRAWN: B.N.
DATE: 9.12.25	CHECKED: H.M.H.
SCALE: 1:10	APPROVED: <i>Hugh M. Halcrow</i>

CLIENT: Khouri Projects	PROJECT: Proposed Multi Dwelling Housing - 6 Units
SITE: Lots 258 & 259 (No. 59-61) Memorial Ave., BLACKWALL	TITLE: BEAM/JOIST CONNECTION DETAILS

DA/1115/2024	DRAWING NUMBER: 24.06.010
No. IN SET: S7 of 9	AMENDMENT: