



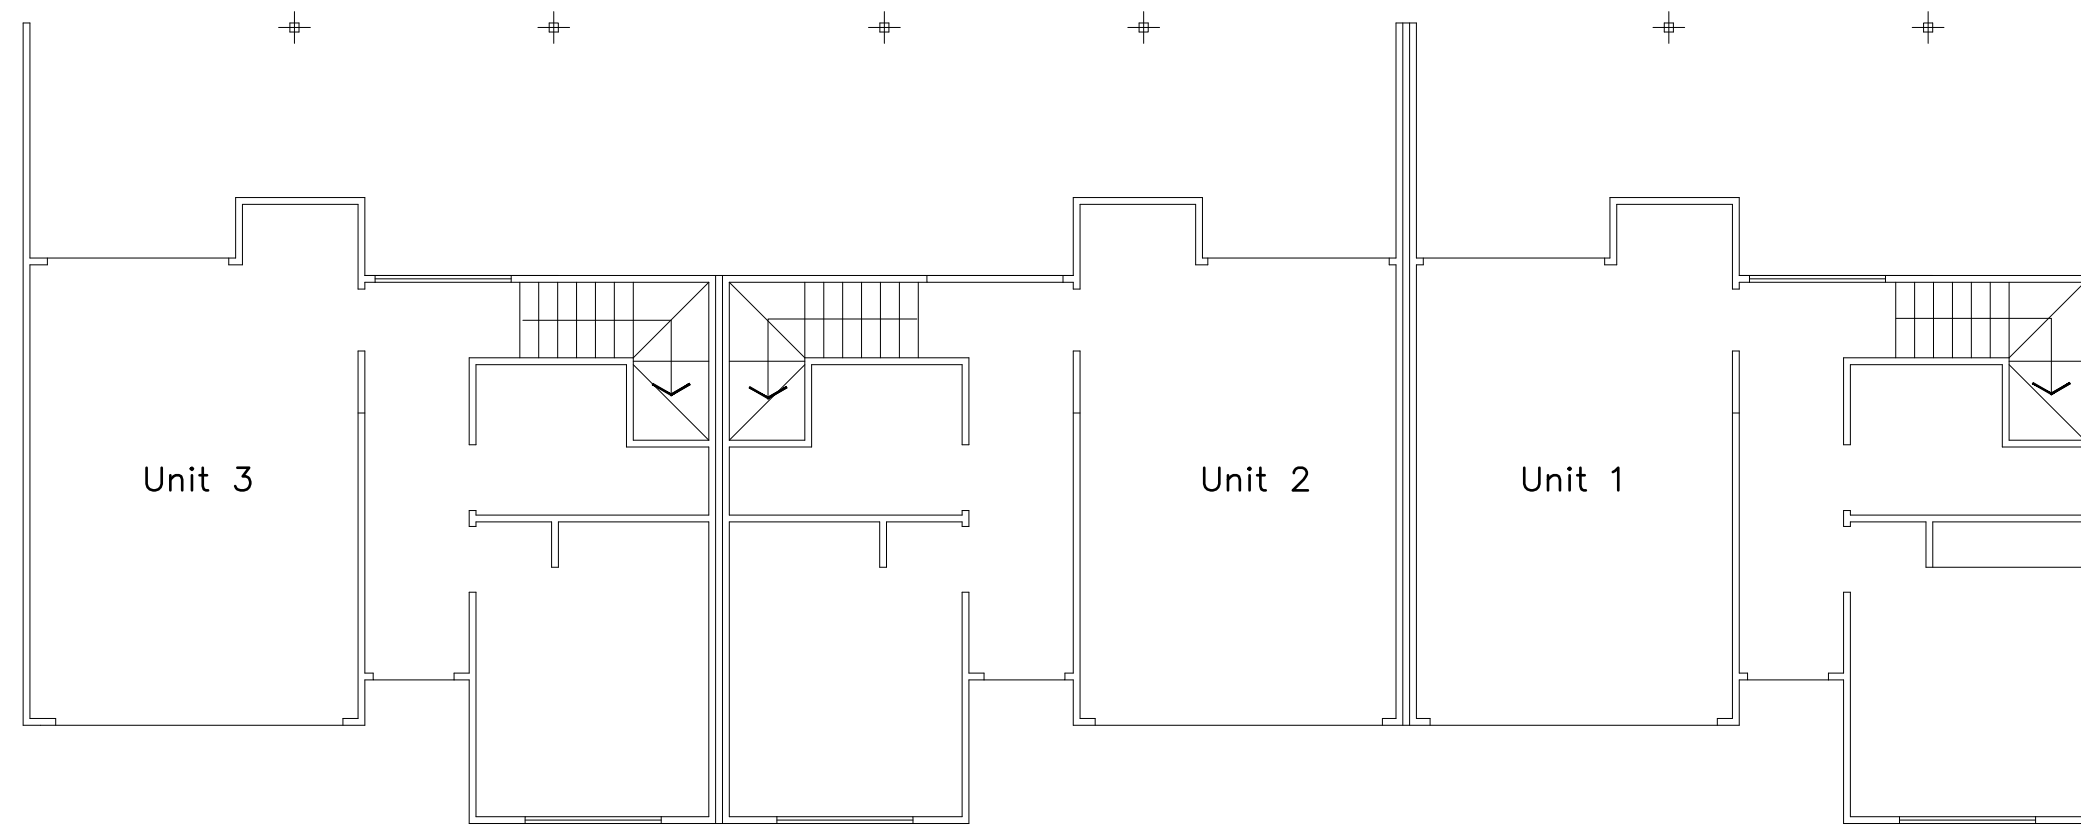

GROUND FLOOR PLAN (1:100)

↑
R = 97 kN bracing capacity required
Provide a minimum of 45 Type A bracing units or
23 Type B bracing units or a combination.


↔ R = 33 kN bracing capacity required
Provide a minimum of 20 Type A bracing units or
10 Type B bracing units in wall frames.

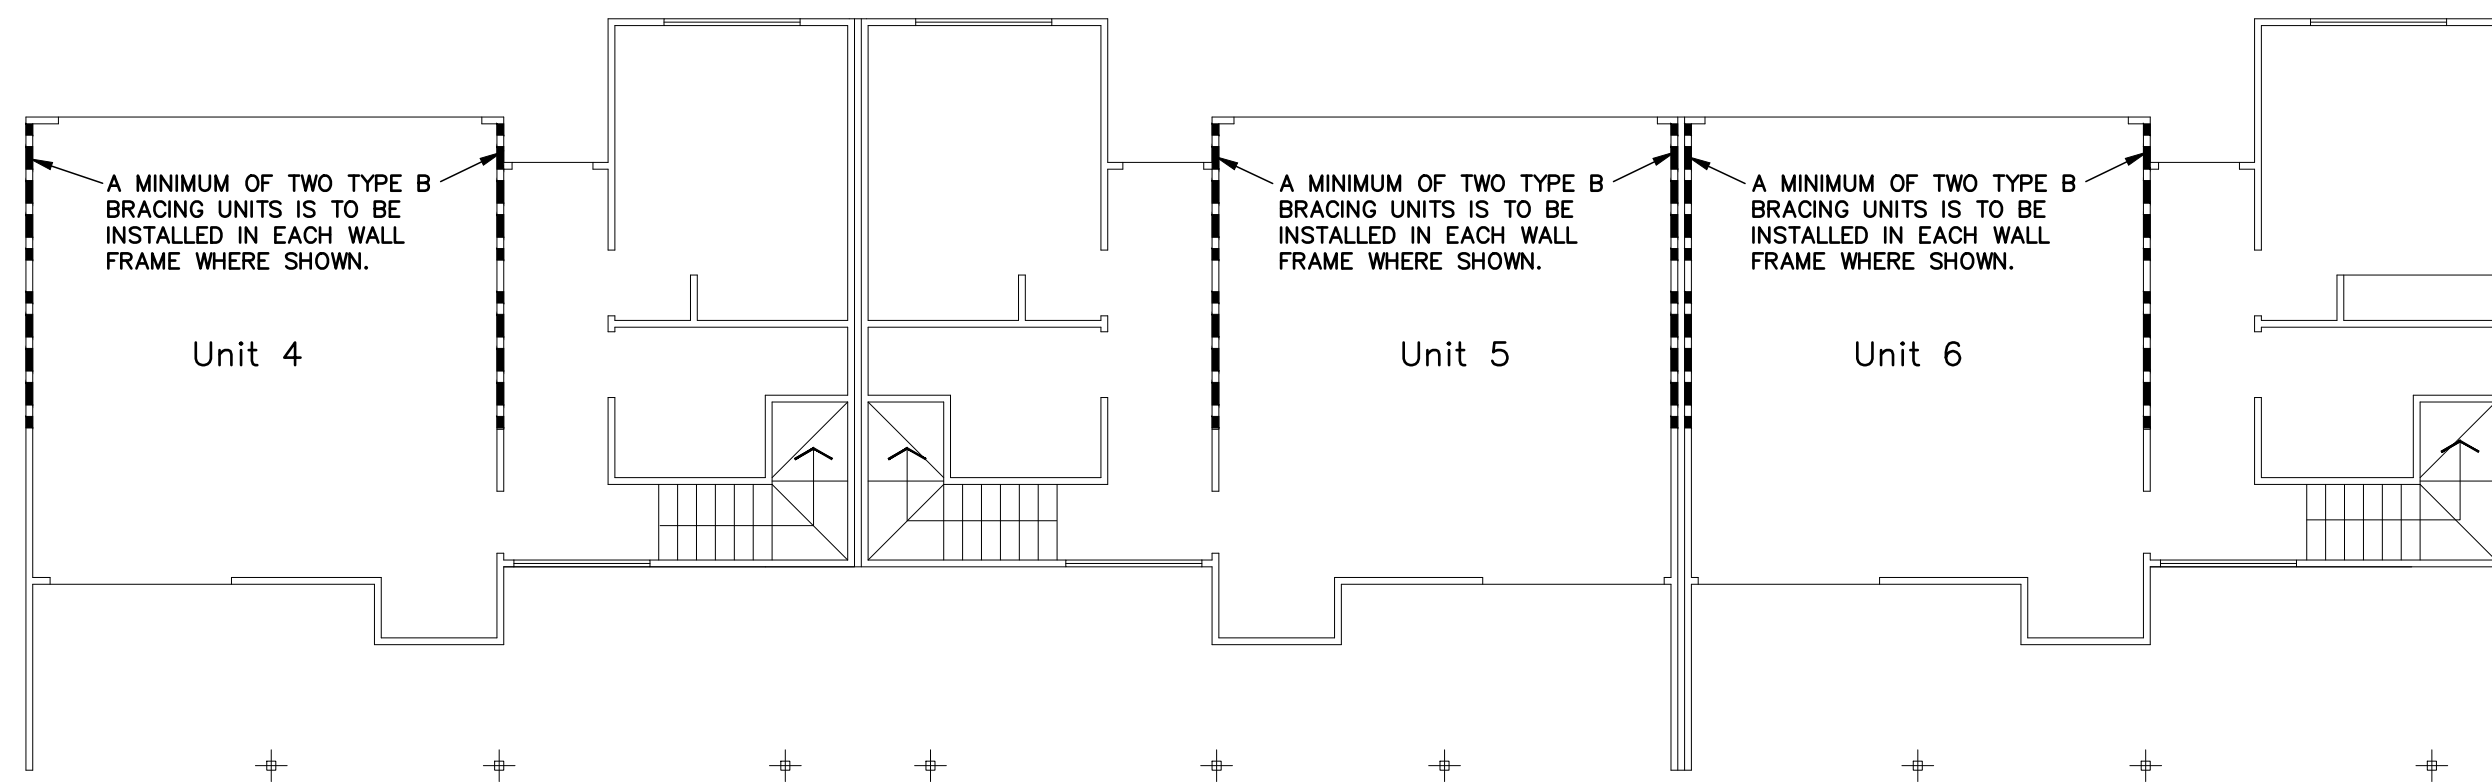

GROUND FLOOR PLAN (1:100)

↑
R = 110 kN bracing capacity required
Provide a minimum of 60 Type A bracing units or
30 Type B bracing units or a combination.


↔ R = 30 kN bracing capacity required
Provide a minimum of 20 Type A bracing units
in wall frames.

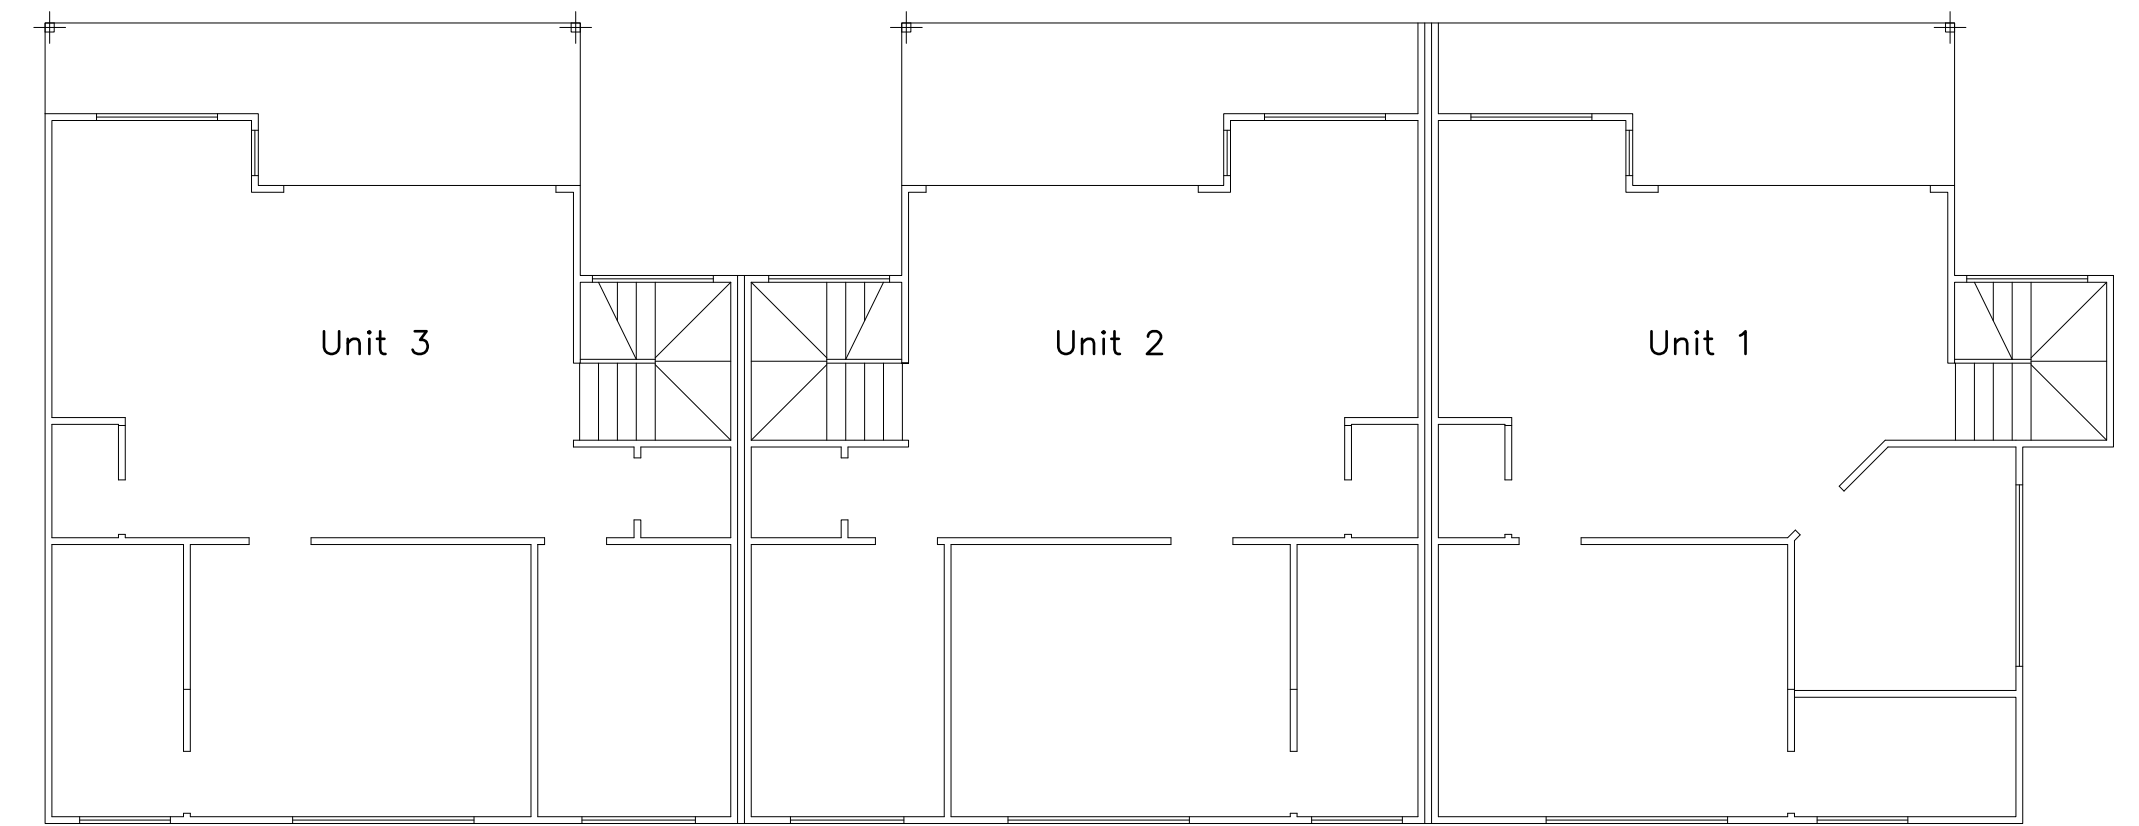

FIRST FLOOR PLAN (1:100)

↑
R = 42 kN bracing capacity required
Provide a minimum of 24 Type A bracing units or
12 Type B bracing units or a combination.

↔ R = 13 kN bracing capacity required
Provide a minimum of 12 Type A bracing units
in wall frames.

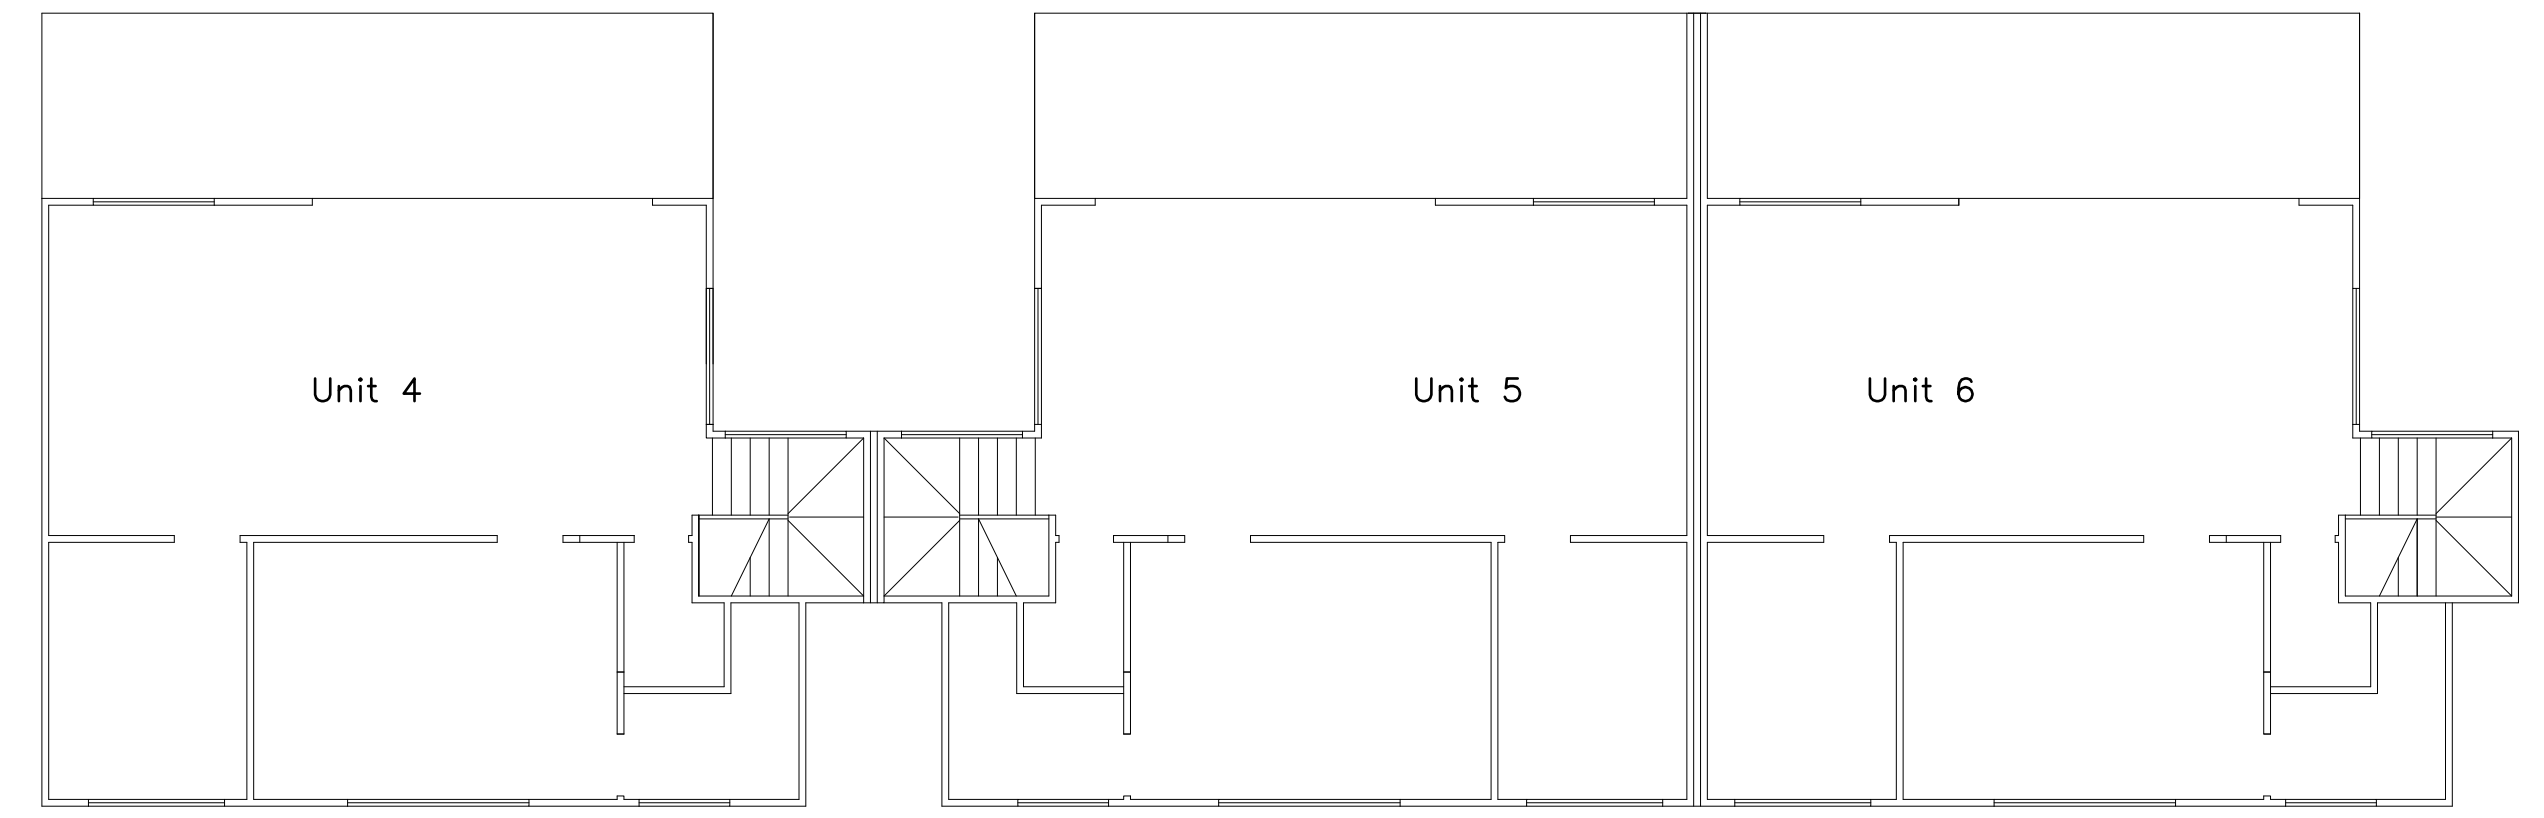

FIRST FLOOR PLAN (1:100)

↑
R = 48 kN bracing capacity required
Provide a minimum of 36 Type A bracing units or
18 Type B bracing units or a combination.

↔ R = 13 kN bracing capacity required
Provide a minimum of 12 Type A bracing units
in wall frames.



ORIGINAL SIZE = A1

HALCROW & ASSOCIATES
CONSULTING STRUCTURAL ENGINEERS
A.C.N. 003 805 374

108 Avoca Drive,
Kincumber, N.S.W. 2251,
P.O. Box 6349 Kincumber, 2251
Phone: (02) 4369-0977
Email: design@halcrow.com.au

DESIGN: H.M.H.	DRAWN: B.N.	CLIENT: Khouri Projects	DRAWING NUMBER: DA/1115/2024
DATE: 30.10.25	CHECKED: HMH	PROJECT: Proposed Multi Dwelling Housing – 6 Units	24.06.010
SCALE: 1:100		SITE: Lots 258 & 259 (No. 59–61) Memorial Ave., BLACKWALL	No. IN SET: 8 of 9
APPROVED: <i>Hugh M. Halcrow</i>	BE MIEAust CPENG	TITLE: BRACING PLAN	AMENDMENT: