
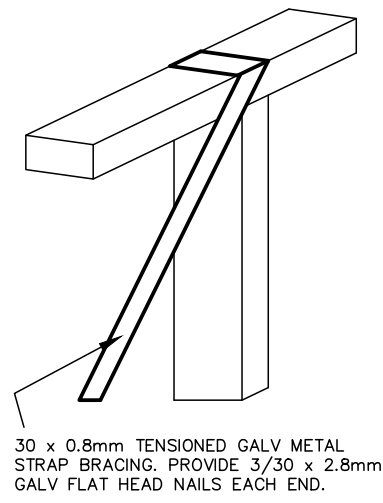


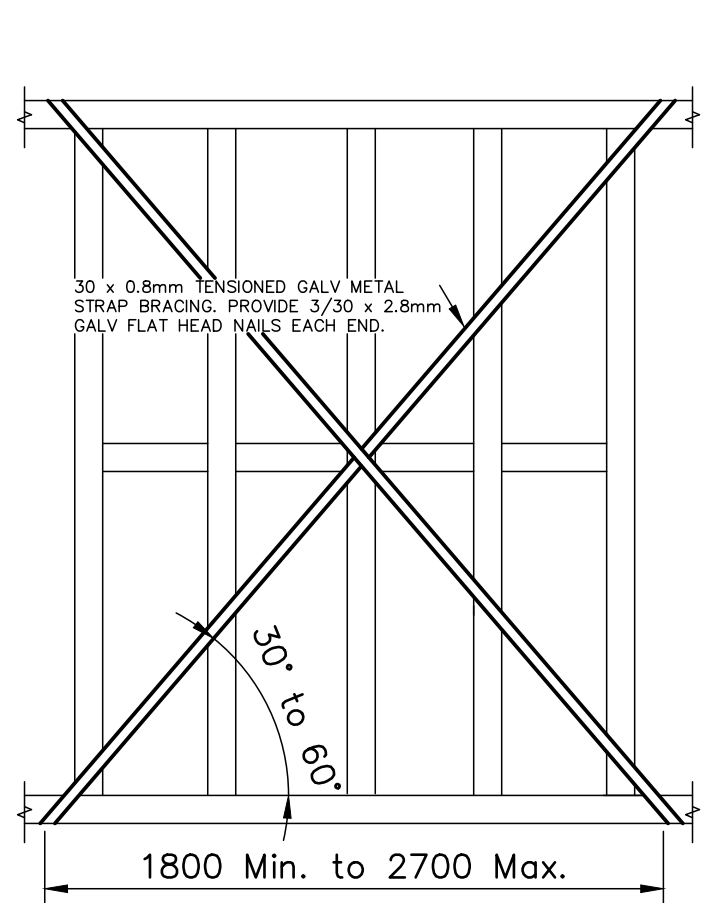



METAL TENSION STRAP BRACING			
MATERIAL & SIZE	NAILING REQUIREMENTS		SPECIAL REQUIREMENTS
	EACH STUD	EACH PLATE	
GALVANISED FLAT TENSION STRAP, 30 x 0.8 mm MIN THICK (15mm ² min)	1/30 x 2.8 GALV. FLAT HEAD NAILS	1/30 x 2.8 GALV. FLAT HEAD NAILS	STRAPS TO BE PAIRED AND OPPOSING. 1.5m MIN TO 2.7 MAX WIDE.

NOTE: STRAPS MUST BE PROPERLY TENSIONED AND STRAP MUST RETURN OVER TOP PLATE AND UNDER BOTTOM PLATE.

METAL STRAP BRACING

Detail 8.18B (AS 1684.2–2006) 1.5 kN/m
Detail 8.3B (AS 1684.4–2006) 1.5 kN/m

BRACING – BR.1 TYPE A

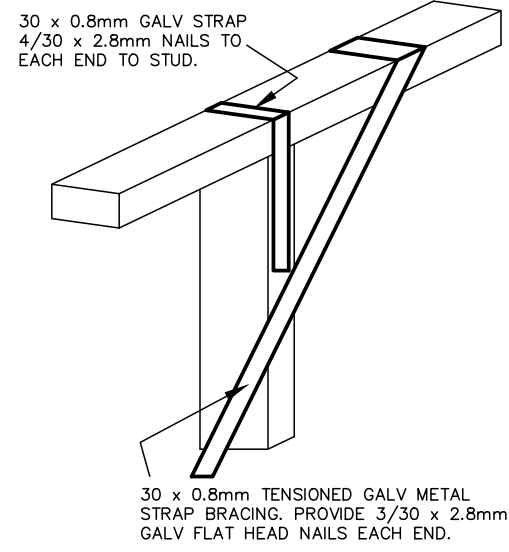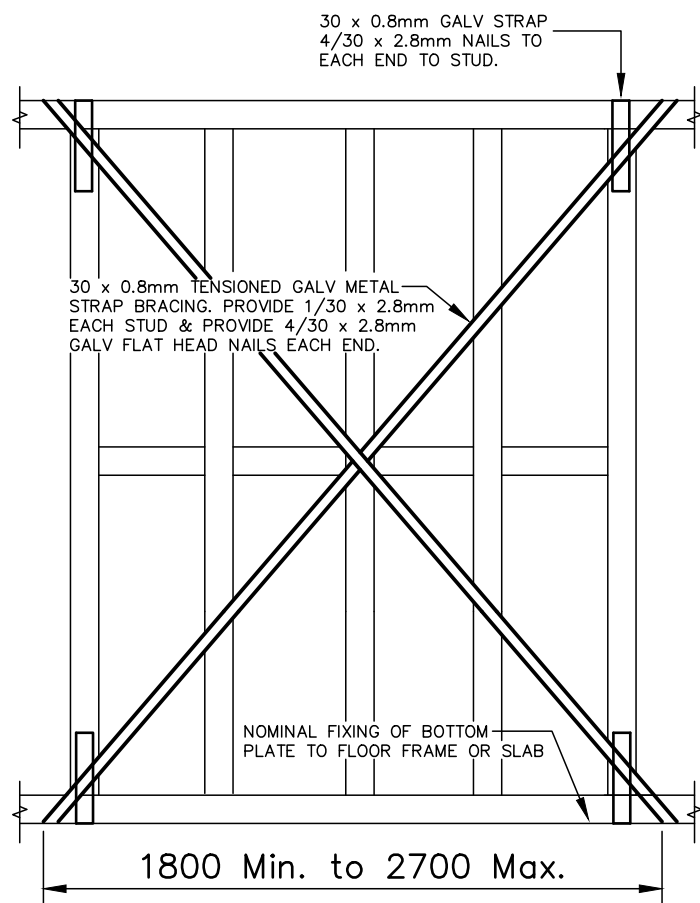


METAL TENSION STRAP BRACING			
MATERIAL & SIZE	NAILING REQUIREMENTS		SPECIAL REQUIREMENTS
	EACH STUD	EACH PLATE	
GALVANISED FLAT TENSION STRAP, 30 x 0.8 (MIN 15 sq.mm)	1/30 x 2.8 GALV. FLAT HEAD NAILS	4/30 x 2.8 GALV. FLAT HEAD NAILS	STRAPS TO BE PAIRED AND OPPOSING. 1.5m MIN TO 2.7 MAX WIDE.

NOTE: STRAPS MUST BE PROPERLY TENSIONED AND STRAP MUST RETURN OVER TOP PLATE AND UNDER BOTTOM PLATE. THE STUD NEAREST TO THE ENDS OF THE DIAGONAL STRAP BRACING SHALL BE FIXED TO THE TOP AND BOTTOM PLATES WITH STRAPS OR FRAMING ANCHORS – 4/30 x 2.8 NAILS EACH END.

METAL STRAP BRACING

Detail 8.18D (AS 1684.2–2006) 3.0 kN/m
Detail 8.3D (AS 1684.4–2006) 3.0 kN/m

BRACING – BR.2 TYPE B

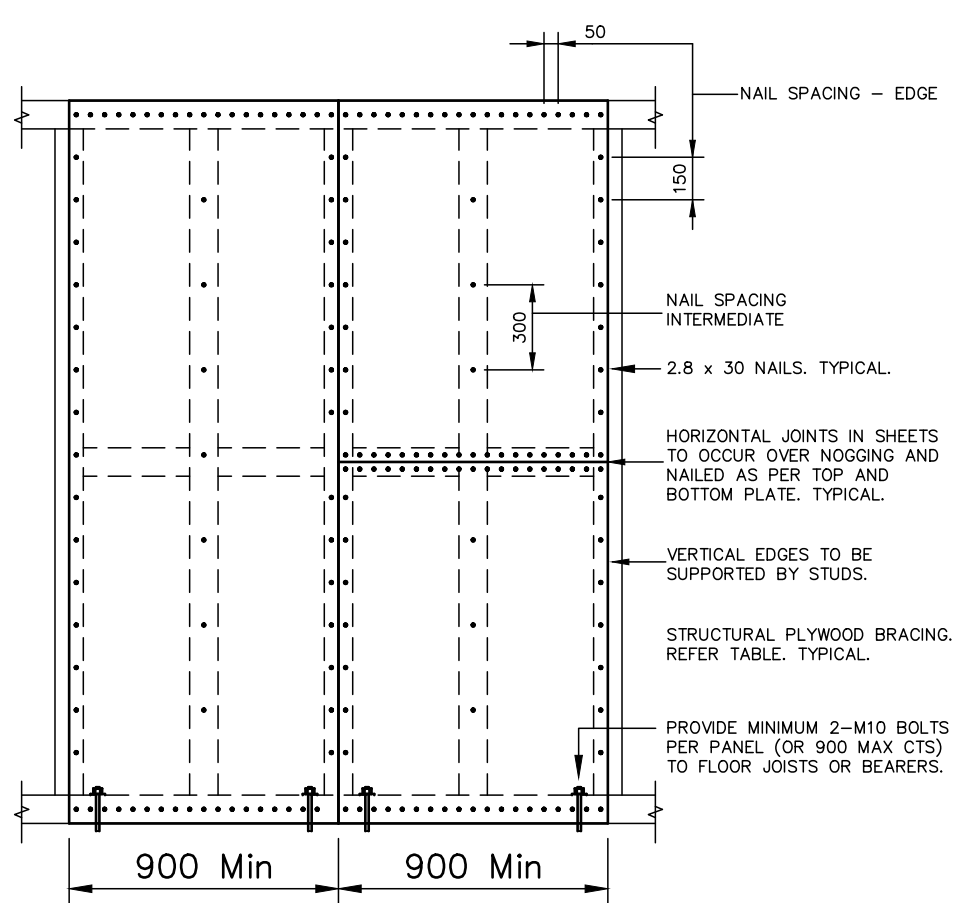

TYPE/ GRADE	MIN. THICKNESS – STUD SPACING		PANEL LENGTH	NAIL SIZE	NAIL SPACING (mm)	
	450	600			EDGE	INTER– MEDIATE
F8	7	9	900 MIN	2.8x30	50 TO PLATES 150 TO EDGE STUDS	300
F11	6	7				
F14	4	6				
F27	4	4.5				

STRUCTURAL PLYWOOD BRACING

Detail 8.18H Method B (AS 1684.2) 6.0 kN/m

BRACING – BR.3 TYPE B

Each 900mm wide panel = one Type B bracing unit.



ORIGINAL SIZE = A1

ISSUE:	DATE:	DETAILS OF AMENDMENT:

HALCROW & ASSOCIATES
CONSULTING STRUCTURAL ENGINEERS
A.C.N. 003 805 374

108 Avoca Drive,
Kincumber, N.S.W. 2251,
P.O. Box 6349 Kincumber, 2251

Phone: (02) 4369-0977
Email: design@halcrow.com.au

DESIGN: H.M.H.	DRAWN: B.N.
DATE: 30.10.25	CHECKED: HMH
SCALE: 1:10	APPROVED: <i>Hugh M. Halcrow</i>
	BE MIEAust CPENG

CLIENT: Khouri Projects	PROJECT: Proposed Multi Dwelling Housing – 6 Units	SITE: Lots 258 & 259 (No. 59–61) Memorial Ave., BLACKWALL	TITLE: BRACING DETAILS
-------------------------	--	---	------------------------

DA/1115/2024

DRAWING NUMBER:

24.06.010

No. IN SET:

S9 of 9

AMENDMENT: