

PROPOSED DOUBLE STOREY DWELLING
#7, Dalgal Street, Austral

PARAGON

Paragon Building Certifiers Pty Ltd

RBC00045

Registered Certifier

APPROVED

Reference: 260471/01

Date: 07/09/2026



Page No	Title
1	Coverpage
2	Safety in Design Notes
3	Building Specification
4	Building Specification
5	Basix Notes
6	Cut and Fill Plan
7	Site Plan
8	Slab Plan
9	Ground Floor Plan
10	First Floor Plan
11	Roof Plan
12	Elevation
13	Side Elevation
14	Section
15	Door Schedule & SOF
16	Window Schedule
17	Landscape Plan
18	Sediment Control Plan
19	GFA Calculation
20	Floor Finish

TERMITE SHEET

-TERMITE SHEET EXTENDS THROUGH THE ENTIRE MASONRY LEAF AND IS
VISIBLE AT THE FINISHED FACE OF THE WALL.

Figure 10.2.29 Typical membrane termination at drainage outlet




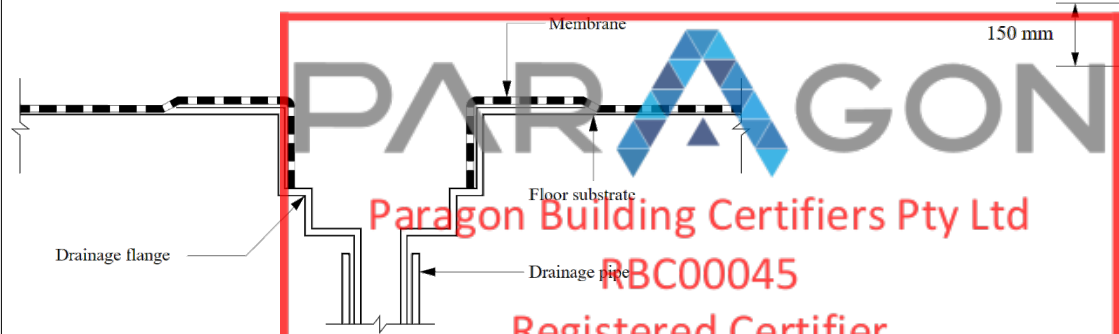


Figure 10.2.24 Typical bathroom door details for whole bathroom waterproofing

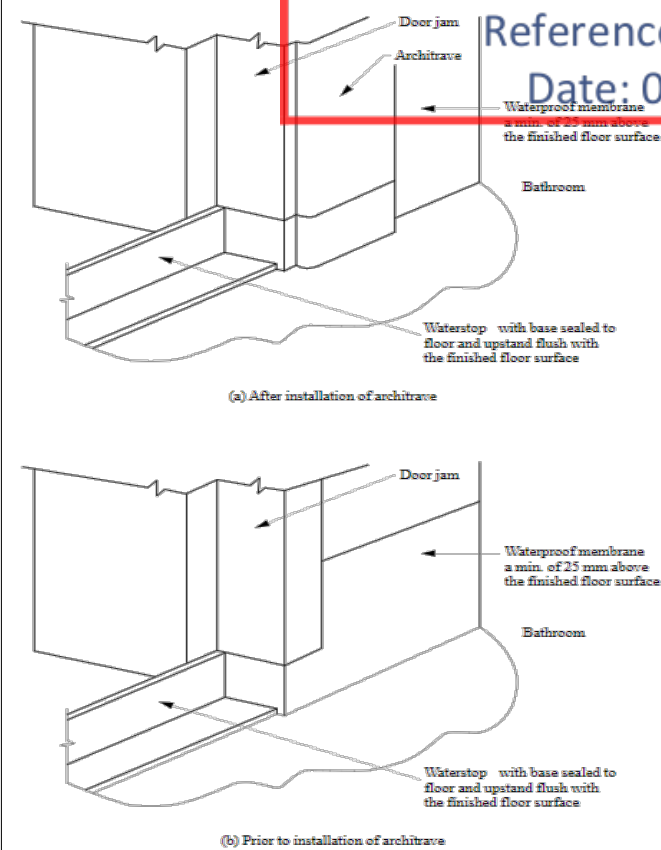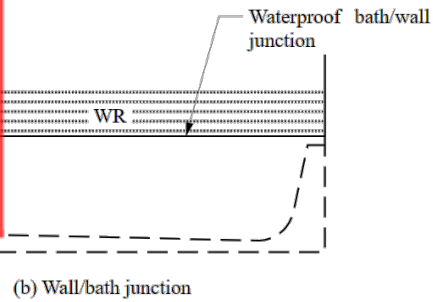

BASIN & BATHTUB:

Figure 10.2.5 Bath and vessel abutting wall — areas to be protected

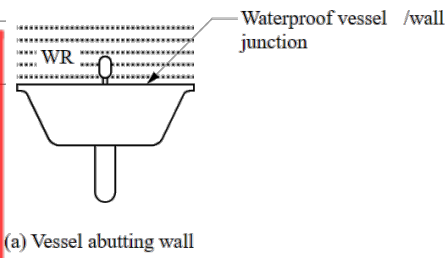

ENCLOSED SHOWER AREA

Figure 10.2.17 Typical hobless construction



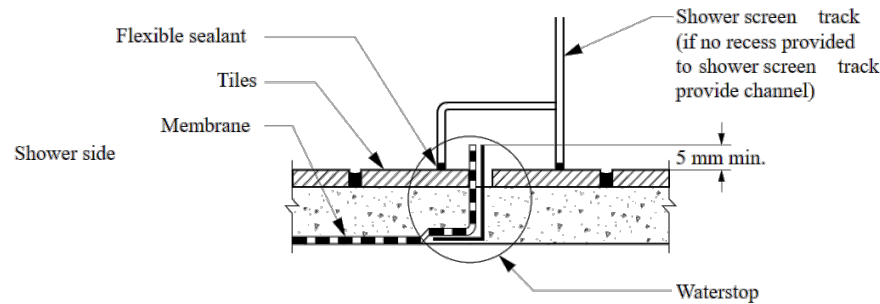


Figure 10.2.16: Typical hob construction — internal membrane

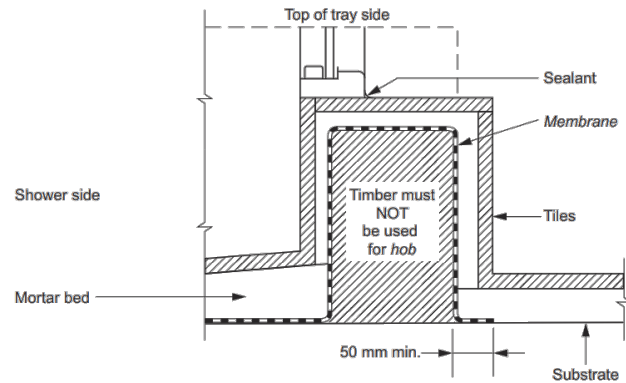

Typical detail of HOB Construction as per BCA ABCB Housing Provisions Part 10.2.16

Figure 10.2.2 Extent of treatment for shower areas — concrete compressed fibre-cement and fibre-cement sheet floors

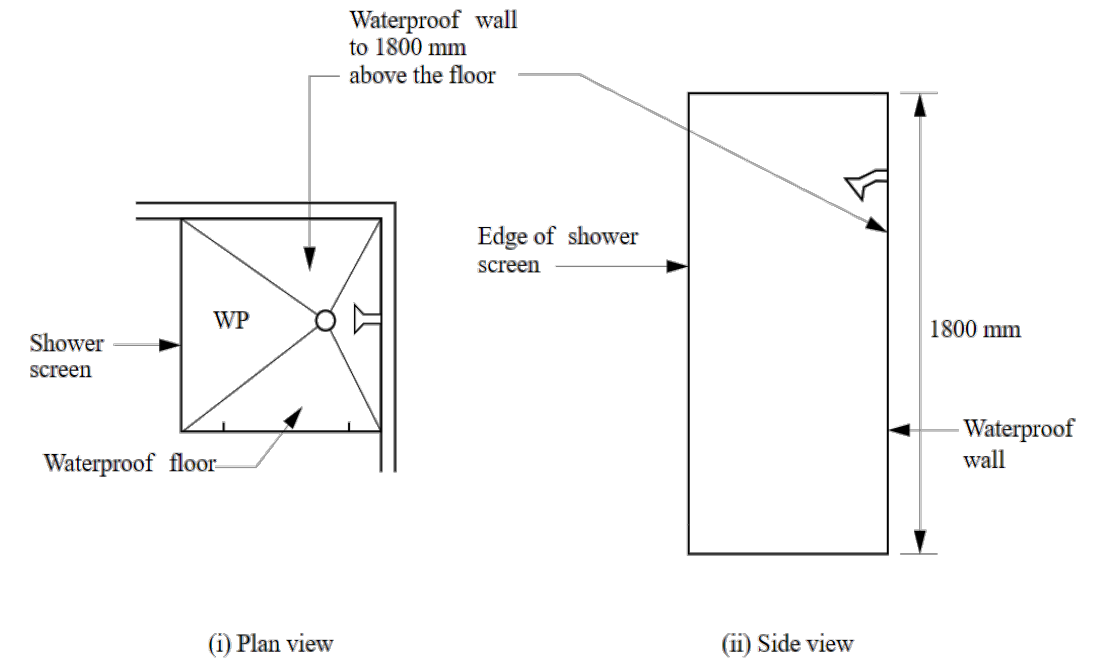

(a) Enclosed shower

Typical detail of enclosed shower as per BCA ABCB Housing Provisions Part 10.2.2

10.2.12 Construction of wet area floors — falls


Where a floor waste is installed—

- (a) the minimum continuous fall of a floor plane to the waste must be 1:80; and
- (b) the maximum continuous fall of a floor plane to the waste must be 1:50.

Floor Waste

app.buildingtools.co

tools

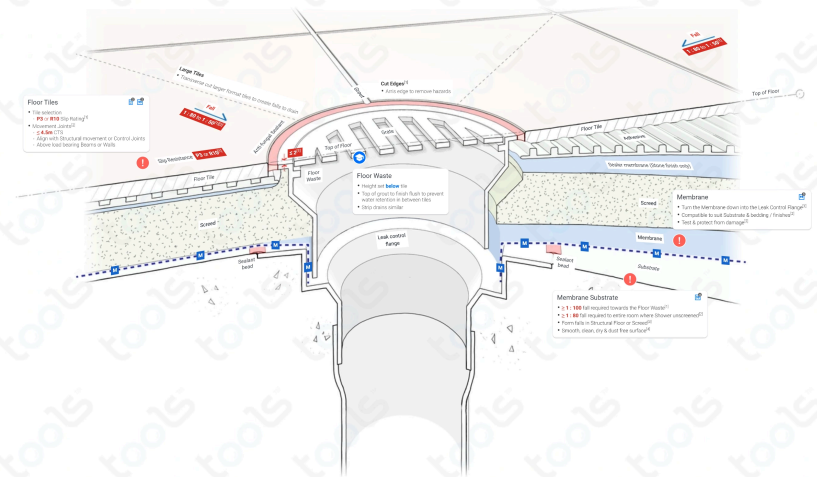

NOTE
The Builder shall check all dimensions and levels on site prior to construction. Notify any errors, discrepancies or omissions to the building designer. Refer to written dimensions only. Do not scale drawings. Drawings shall not be used for construction purposes until issued for construction. This drawing reflects a design by Innovative Eco Designs and is to be used only for work when authorised in writing by Innovative Eco Designs.
All boundaries and contours are subject to survey drawing. All levels to Australian Height Data. It is the contractors responsibility to confirm all measurements on site and locations of any services prior to work on site.
All documents here within are subject to Australian Copyright Laws.



37604191460 ABN
(02) 8710 3852
SUITE 7, 4-10 SELEMS PDE
REVESBY, NSW, 2212
design@iedesigns.com.au
www.iedesigns.com.au



B	21-08-2026	Issue for CDC
A	02/08/2026	Issue for CDC

DRAWING : **Building Specification**
CLIENT : **Sandstone Constructions Pty Ltd**
PROJECT : **PROPOSED DOUBLE STOREY DWELLING**
#7,Dalgat Street,Austral
Lot-612 D.P 1295393

DRAWN BY: NB
SCALE: APPLICATION : CDC
PAGE SIZE A3
PAGE NO: 3
PROJECT NO. **2606 920**
ISSUE **B**

TERMITE SHEET


- TERMITE SHEET EXTENDS THROUGH THE ENTIRE MASONRY LEAF AND IS VISIBLE AT THE FINISHED FACE OF THE WALL.



FIGURE 5.5 (in part) TYPICAL SHEET INSTALLATION TO EXTERNAL WALL WITH CONCRETE FLOOR SLAB

DPC FOR BRICKS

DAMP-PROOF COURSE (DPC) TO EXTENDS THROUGH THE ENTIRE MASONRY LEAF AND NEED TO BE VISIBLE AT THE FINISHED FACE OF THE WALL FROM OUTSIDE

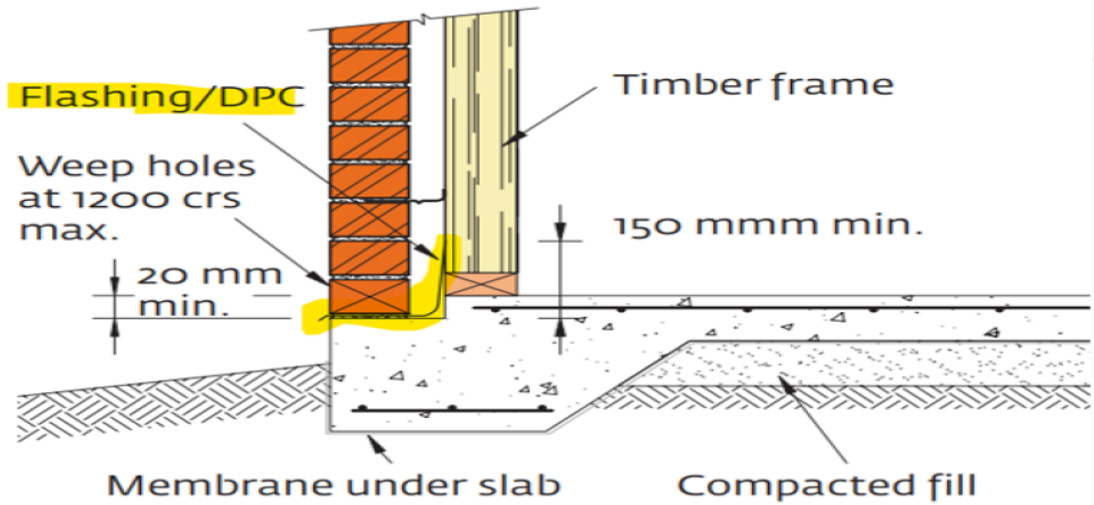

NOTE
The Builder shall check all dimensions and levels on site prior to construction. Notify any errors, discrepancies or omissions to the building designer. Refer to written dimensions only. Do not scale drawings. Drawings shall not be used for construction purposes until issued for construction. This drawing reflects a design by Innovative Eco Designs and is to be used only for work when authorised in writing by Innovative Eco Designs.
All boundaries and contours are subject to survey drawing. All levels to Australian Height Data. It is the contractors responsibility to confirm all measurements on site and locations of any services prior to work on site.
All documents here within are subject to Australian Copyright Laws.



37604191460 ABN
(02) 8710 3852
SUITE 7, 4-10 SELEMS PDE
REVESBY, NSW, 2212
design@iedesigns.com.au
www.iedesigns.com.au



B	21-08-2026	Issue for CDC
A	02/08/2026	Issue for CDC

Figure 10.8.3 (explanatory) Example of roof space with low level ventilation


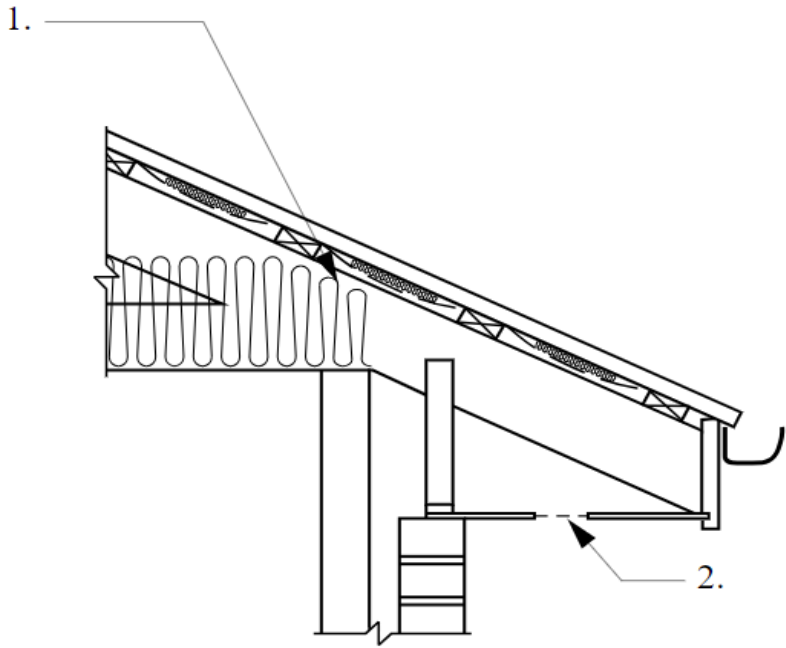


Figure Notes

- (1) Minimum 20 mm gap maintained between insulation and sarking.
(2) Eave ventilation opening in accordance with Table 10.8.3.

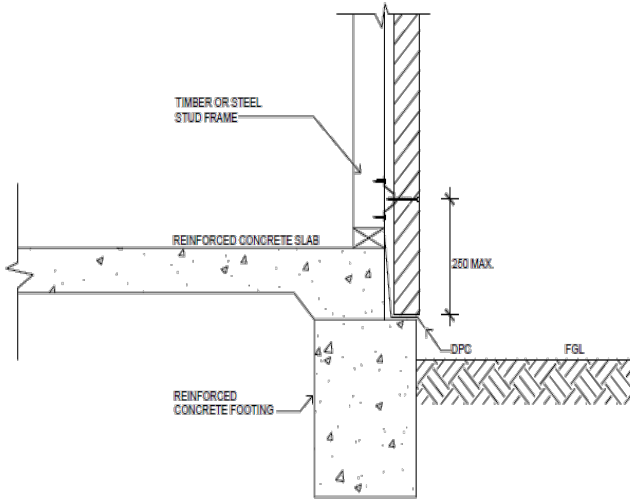

10.8.3


Ventilation of roof spaces

[2019: 3.8.7.4]

- (1) In *climate zones* 6, 7 and 8, a roof must have a roof space that—
- (a) is located—
- (i) immediately above the *primary insulation layer*; or
- (ii) immediately above sarking with a *vapour permeance* of not less than 1.14 µg/N.s, which is immediately above the *primary insulation layer*; or
- (iii) immediately above ceiling insulation that meets the requirements of 13.2.3(3) and 13.2.3(4); and
- (b) has a height of not less than 20 mm; and
- (c) is either—
- (i) ventilated to *outdoor air* through evenly distributed openings in accordance with Table 10.8.3; or
- (ii) located immediately underneath the roof tiles of an unsarked tiled roof.
- (2) The requirements of (1) do not apply to a—
- (a) concrete roof; or
- (b) roof that is made of structural insulated panels; or
- (c) roof that is subject to Bushfire Attack Level FZ requirements in accordance with AS 3959.

Table 10.8.3: Roof space ventilation requirements

Roof pitch	Ventilation openings
< 10°	25,000 mm ² /m provided at each of two opposing ends
≥ 10° and < 15°	25,000 mm ² /m provided at the eaves and 5,000 mm ² /m at high level
≥ 15° and < 75°	7,000 mm ² /m provided at the eaves and 5,000 mm ² /m at high level, plus an additional 18,000 mm ² /m at the eaves if the roof has a cathedral ceiling

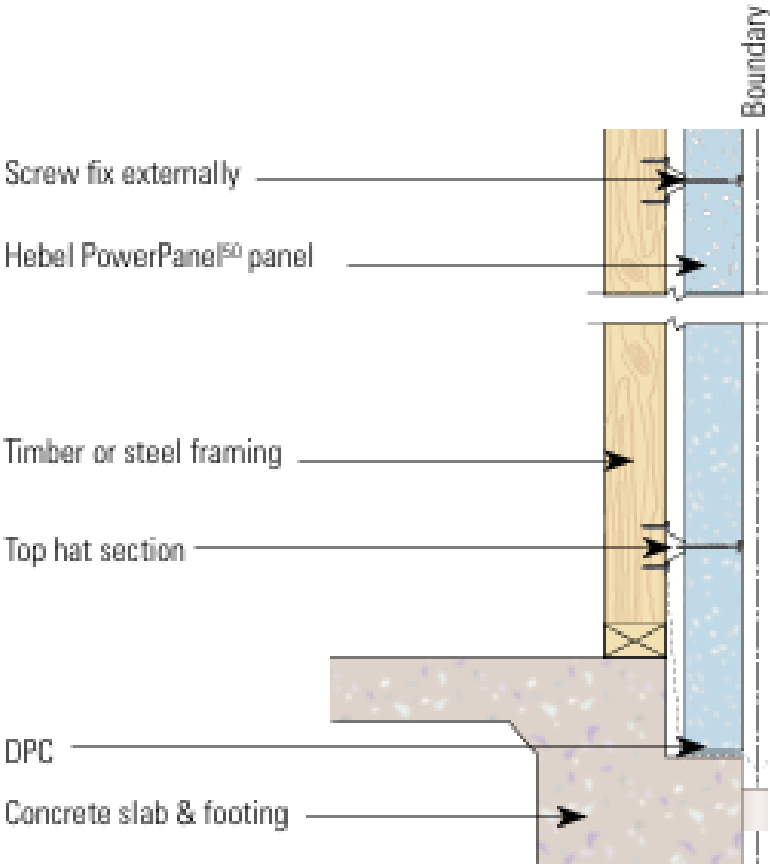

BASIX™ Certificate

Building Sustainability Index
www.planningportal.nsw.gov.au/development-and-assessment/basix

Single Dwelling

Certificate number: 1861977S
Paragon Building Certifiers Pty Ltd

This certificate confirms that the proposed development will meet the NSW government's requirements for sustainability, if it is built in accordance with the commitments set out below. Terms used in this certificate, or in the commitments, have the meaning given by the document entitled "BASIX Definitions" dated 10/09/2020 published by the Department. This document is available at www.planningportal.nsw.gov.au/definitions
Reference: 260471/01
Date: 07/09/2026
Secretary
Date of issue: Thursday, 20 August 2026
To be valid, this certificate must be submitted with a development application or lodged with a complying development certificate application within 3 months of the date of issue.



Basix-Commitments

/for details: See the Basix certificate/

Alternative water
The applicant must install a rainwater tank of at least 2000 litres.
The rainwater tank to collect rain runoff from at least 150 m2 of the roof
The applicant must connect the rainwater tank to:
• all toilets in the development
• at least one outdoor tap in the development

- Fixtures
- Shower heads 4 star (>6.0 but <= 7.5 L/min)
 - Toilets.....3 star
 - Kitchen tap.....3 star
 - Basin Taps.....3 star

Hot Water System: gas instantaneous with a performance of 6.0 stars /or a system with a higher energy rating/

Heating/Cooling: In at least 1 living area and 1 bedroom: 1-phase Air-conditioning; Energy rating: 3 STAR (average zone)

- Ventilation
- At least 1 Bathroom: individual fan, ducted to façade ; Operation control:manual switch on/off
 - Kitchen: individual fan, ducted to façade ; Operation control: manual switch on/off
 - Laundry: natural ventilation only, or no laundry; Operation control: n/a

- Natural lighting
- The applicant must install a window and/or skylight in the kitchen of the dwelling for natural lighting.
 - The applicant must install a window and/or skylight in 1 bathroom(s)/toilet(s) in the development for natural lighting.

- Artificial lighting fluorescent
- The applicant must ensure that a minimum of 80% of light fixtures are fitted with fluorescent, compact fluorescent, or light-emitting-diode (LED) lamps.

- OTHER
- The applicant must install a gas cook top & electric oven in the kitchen of the dwelling.
 - The applicant must install a fixed outdoor clothes drying line as part of the development.

.



NOTE
The Builder shall check all dimensions and levels on site prior to construction. Notify any errors, discrepancies or omissions to the building designer. Refer to written dimensions only. Do not scale drawings. Drawings shall not be used for construction purposes until issued for construction. This drawing reflects a design by Innovative Eco Designs and is to be used only for work when authorised in writing by Innovative Eco Designs.
All boundaries and contours are subject to survey drawing. All levels to Australian Height Data. It is the contractors responsibility to confirm all measurements on site and locations of any services prior to work on site.
All documents here within are subject to Australian Copyright Laws.



37604191460 ABN
(02) 8710 3852
SUITE 7, 4-10 SELEMS PDE
REVESBY, NSW, 2212
design@iedesigns.com.au
www.iedesigns.com.au



B	21-08-2026	Issue for CDC
A	02/08/2026	Issue for CDC

DRAWING : Basix Notes
CLIENT : Sandstone Constructions Pty Ltd
PROJECT : PROPOSED DOUBLE STOREY DWELLING #7,Dalgai Street,Austral Lot-612 D.P 1295393

DRAWN BY: NB	DATE : 21-08-2026	PROJECT NO. 2606 920
SCALE:	APPLICATION : CDC	ISSUE B
PAGE SIZE A3	PAGE NO: 5	

Cut and Fill is only under Slab.
Cut and Fill on the site is minimal, Hence does not
required Retaining wall.

PARAGON

Paragon Building Certifiers Pty Ltd


RBC00045

Registered Certifier

APPROVED

Reference: 260471/01

Date: 07/09/2026

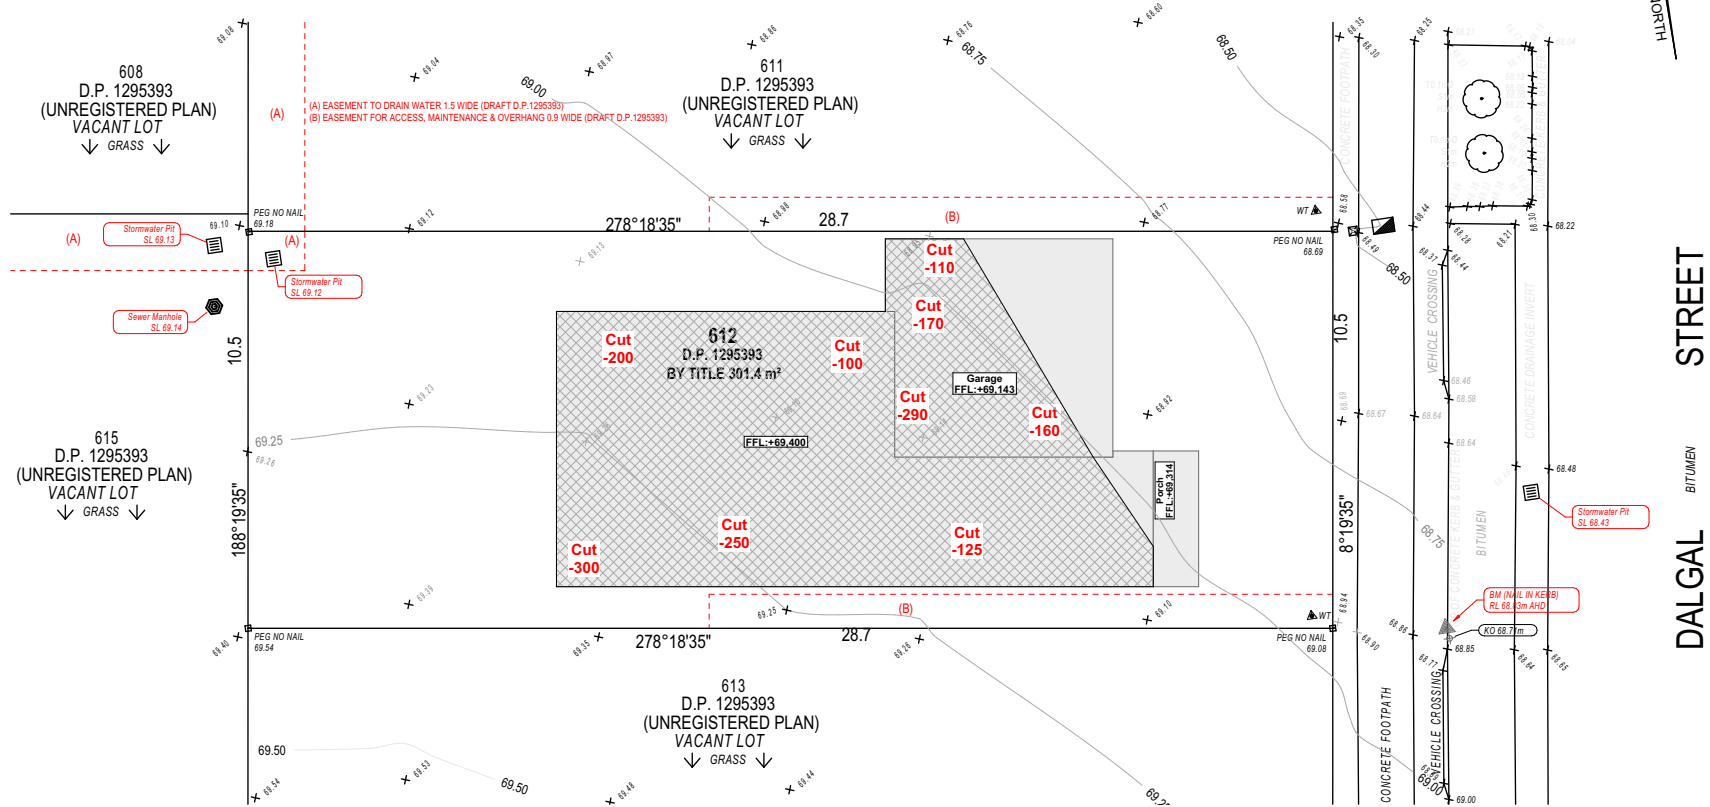

Cut and Fill Plan
1:200



NOTE
The Builder shall check all dimensions and levels on site prior to construction. Notify any errors, discrepancies or omissions to the building designer. Refer to written dimensions only. Do not scale drawings. Drawings shall not be used for construction purposes until issued for construction. This drawing reflects a design by Innovative Eco Designs and is to be used only for work when authorised in writing by Innovative Eco Designs.

All boundaries and contours are subject to survey drawing. All levels to Australian Height Data. It is the contractors responsibility to confirm all measurements on site and locations of any services prior to work on site.

All documents here within are subject to Australian Copyright Laws.



37604191460 ABN
(02) 8710 3852
SUITE 7, 4-10 SELEMS PDE
REVESBY, NSW, 2212
design@iedesigns.com.au
www.iedesigns.com.au



B	21-08-2026	Issue for CDC
A	02/08/2026	Issue for CDC

DRAWING : **Cut and Fill Plan**


CLIENT : **Sandstone Constructions Pty Ltd**

PROJECT : **PROPOSED DOUBLE STOREY DWELLING**
#7,Dalgai Street,Austral
Lot-612 D.P 1295393

DRAWN BY: NB	DATE : 21-08-2026	PROJECT NO. 2606 920
SCALE: 1:200	APPLICATION : CDC	ISSUE B
PAGE SIZE A3	PAGE NO: 6	

Site Calculations			
No.	Name	Area SQM	% of Total Site Area
01	Total Site Area	301.40	100
02	Total Landscape area	114.16	38
03	Area forward of the building line	47.25	16
04	Landscape area forward of the building line	18.79	6
05	Landscape area Behind of the building line	95.37	32
06	Articulation	3.41	---

Gross Floor Area		
No	Name	Area SQM
01	Ground floor	93.70
02	First floor	83.96
		177.66 m ²

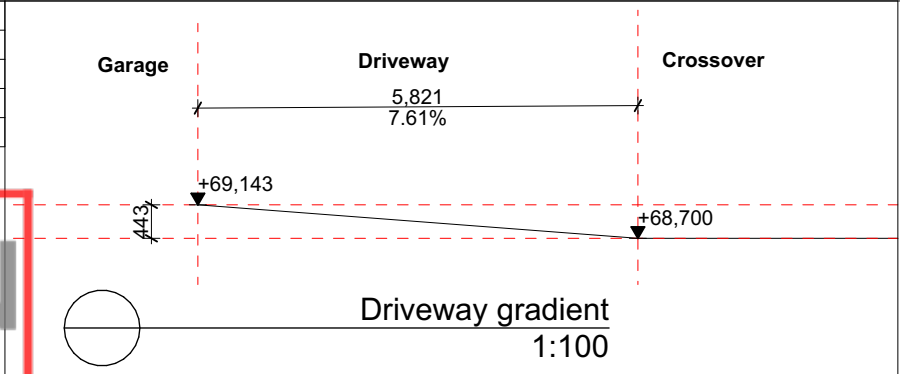

As per 88b, condition no.13 point 4 no building shall be erected or permitted to remain erected on any lot burdened having roof other than Clay tiles, Cement tiles, Slate or non reflective surface corrugated iron. All roofing materials shall be black or shades of grey or natural colours only.

As per section 88b restriction number 11, the lots hereby burdened must be maintained as an Asset Protection Zone (Inner Protection Area) in accordance with Section A4.1.1 of 'Planning for Bushfire Protection 2019' and the NSW Rural Fire Services document 'Standards for Asset Protection Zones.'

PARAGON

Paragon Building Certifiers Pty Ltd


RBC00045

Registered Certifier

APPROVED

Reference: 260471/01

Date: 07/09/2026

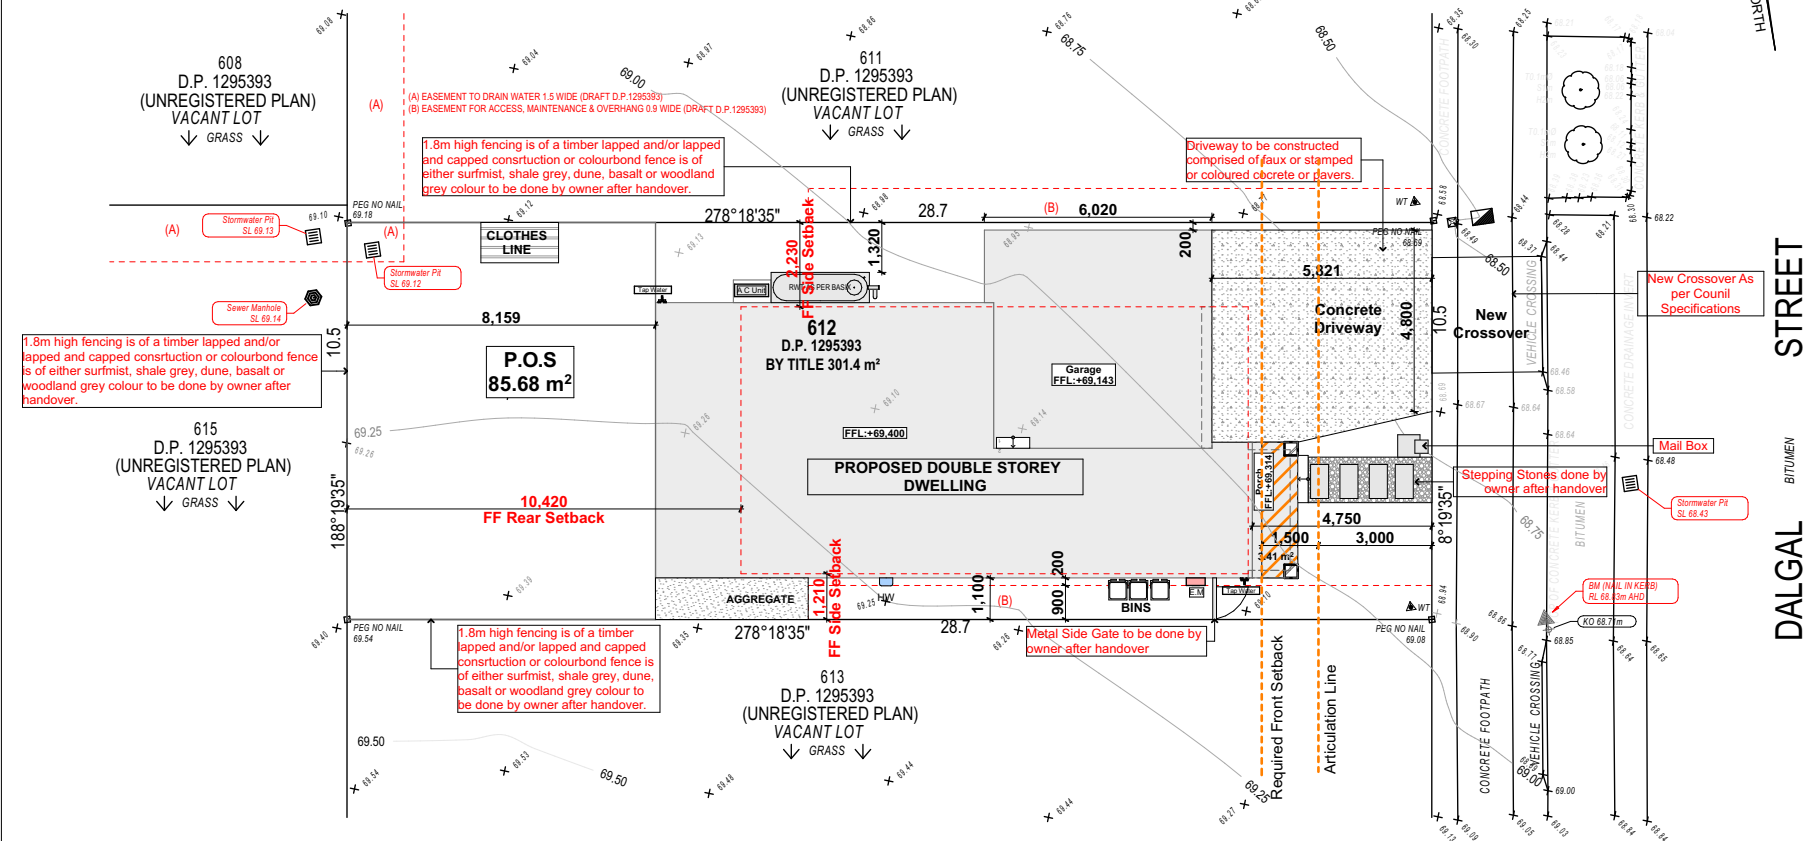

BEFORE
YOU DIG

www.byda.com.au

Zero Damage - Zero Harm

NOTE
The Builder shall check all dimensions and levels on site prior to construction. Notify any errors, discrepancies or omissions to the building designer. Refer to written dimensions only. Do not scale drawings. Drawings shall not be used for construction purposes until issued for construction. This drawing reflects a design by Innovative Eco Designs and is to be used only for work when authorised in writing by Innovative Eco Designs.

All boundaries and contours are subject to survey drawing. All levels to Australian Height Data. It is the contractors responsibility to confirm all measurements on site and locations of any services prior to work on site.

All documents here within are subject to Australian Copyright Laws.

INNOVATIVE
ECO DESIGNS

Your Home Your Style

37604191460 ABN
(02) 8710 3852

SUITE 7, 4-10 SELEMS PDE
REVESBY, NSW, 2212


design@iedesigns.com.au

www.iedesigns.com.au

bdaa

ACCREDITED
BUILDING DESIGNER

B	21-08-2026	Issue for CDC
A	02/08/2026	Issue for CDC

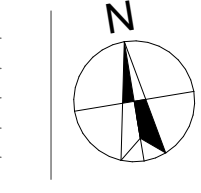


DRAWING : **Site Plan**

CLIENT : **Sandstone Constructions Pty Ltd**

PROJECT : **PROPOSED DOUBLE STOREY DWELLING**
#7,Dalgal Street,Austral
Lot-612 D.P 1295393

DRAWN BY: NB	DATE : 21-08-2026	PROJECT NO. 2606 920
SCALE: 1:200	APPLICATION : CDC	ISSUE B
PAGE SIZE A3	PAGE NO: 7	

- CONCRETE SLAB AS PER ENGINEERS DETAILS
- CONCRETE FOOTINGS AS PER ENGINEER'S DETAILS
- EDGE BEAM DETAILS AS PER ENGINEER'S DETAILS
- ALL BRICK REBATES AS PER ENGINEER'S DETAILS

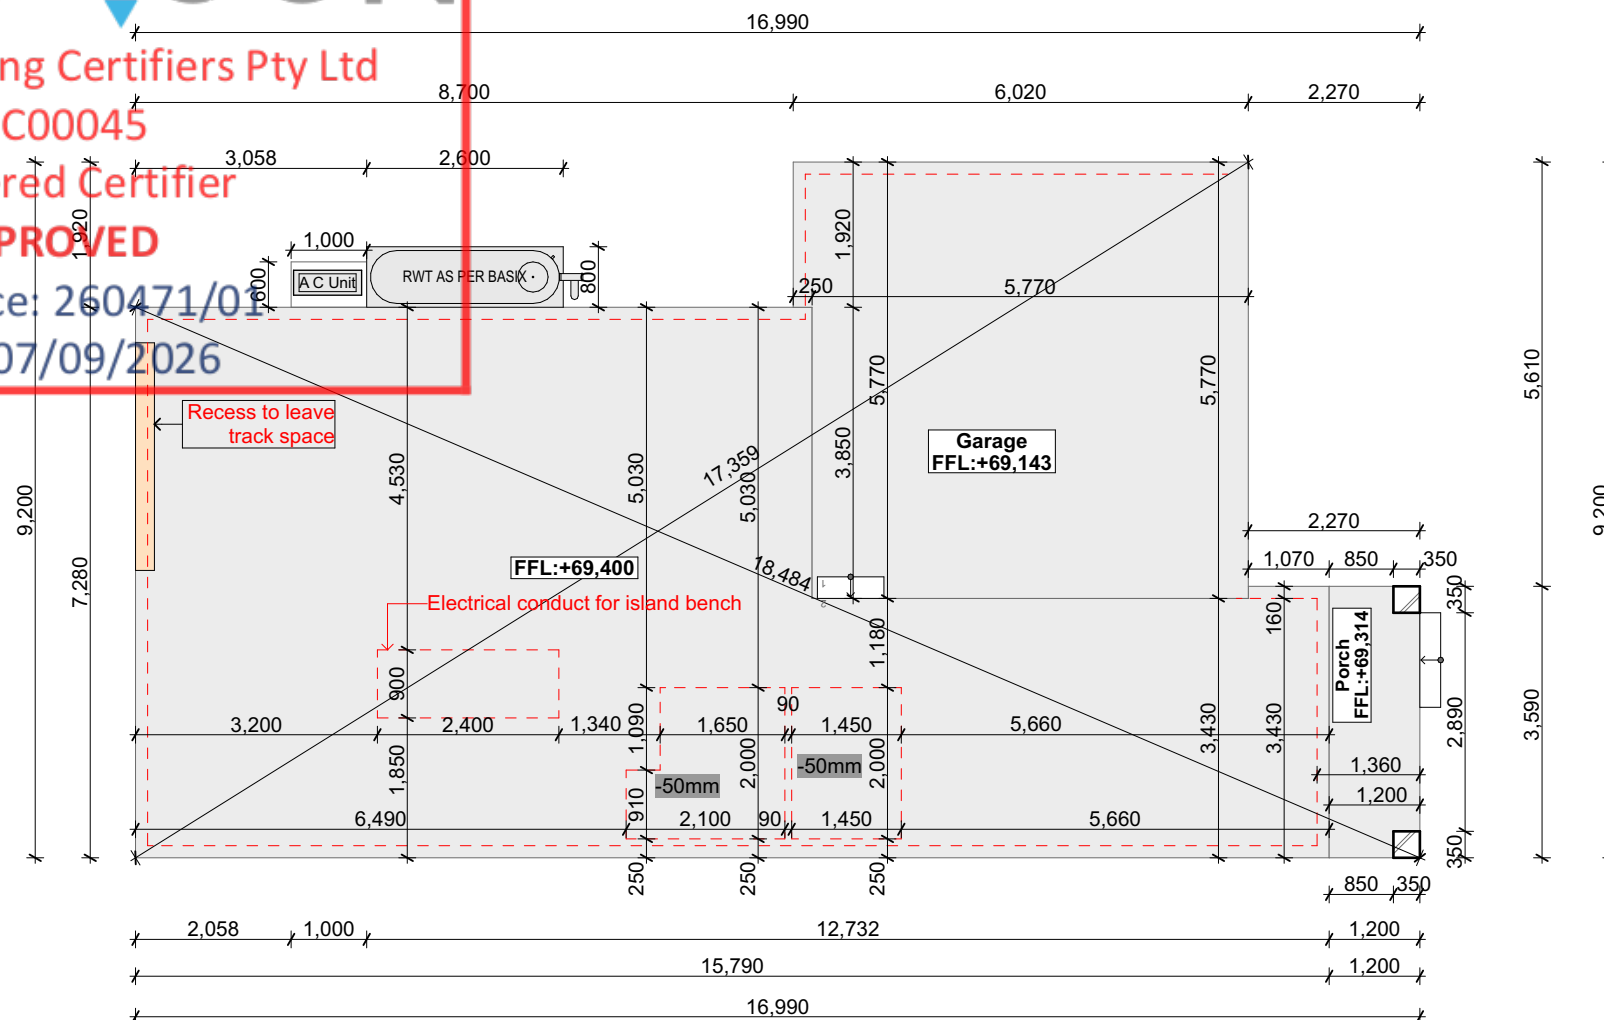

 **BEFORE
YOU DIG**
www.byda.com.au
Zero Damage - Zero Harm



**INNOVATIVE
ECO DESIGNS**
Your Home Your Style





ACCREDITED
BUILDING DESIGNER

DRAWN BY: NB	DATE : 21-08-2026	PROJECT NO. 2606 920
SCALE: 1:100	APPLICATION : CDC	ISSUE B
PAGE SIZE A3	PAGE NO: 8	

External Walls with vapour permeable membrane as per manufacturer detail.

As per 88b, condition no.13 point 4 no building shall be erected or permitted to remain erected on any lot burdened having roof other than Clay tiles, Cement tiles, Slate or non reflective surface corrugated iron. All roofing materials shall be black or shades of grey or natural colours only.

As per section 88b restriction number 11, the lots hereby burdened must be maintained as an Asset Protection Zone (Inner Protection Area) in accordance with Section A4.1.1 of 'Planning for Bushfire Protection 2019' and the NSW Rural Fire Services document 'Standards for Asset Protection Zones.

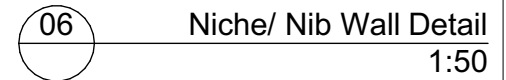
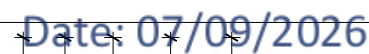


DRAWN BY: NB	DATE : 21-08-2026	PROJECT NO. 2606 920
SCALE: 1:100	APPLICATION : CDC	ISSUE B
PAGE SIZE A3	PAGE NO : 9	

Selected Cladding with vapour permeable membrane as per manufacturer detail.

As per 88b, condition no.13 point 4 no building shall be erected or permitted to remain erected on any lot burdened having roof other than Clay tiles, Cement tiles, Slate or non reflective surface corrugated iron. All roofing materials shall be black or shades of grey or natural colours only.

As per section 88b restriction number 11, the lots hereby burdened must be maintained as an Asset Protection Zone (Inner Protection Area) in accordance with Section A4.1.1 of 'Planning for Bushfire Protection 2019' and the NSW Rural Fire Services document 'Standards for Asset Protection Zones.

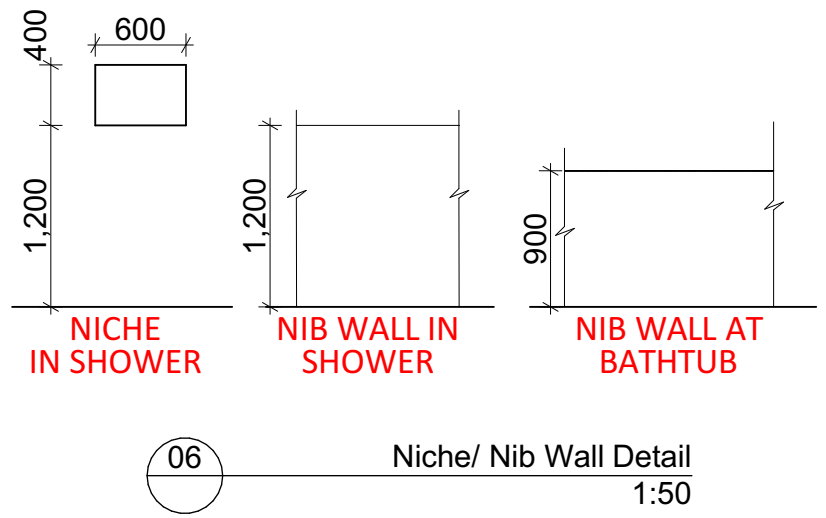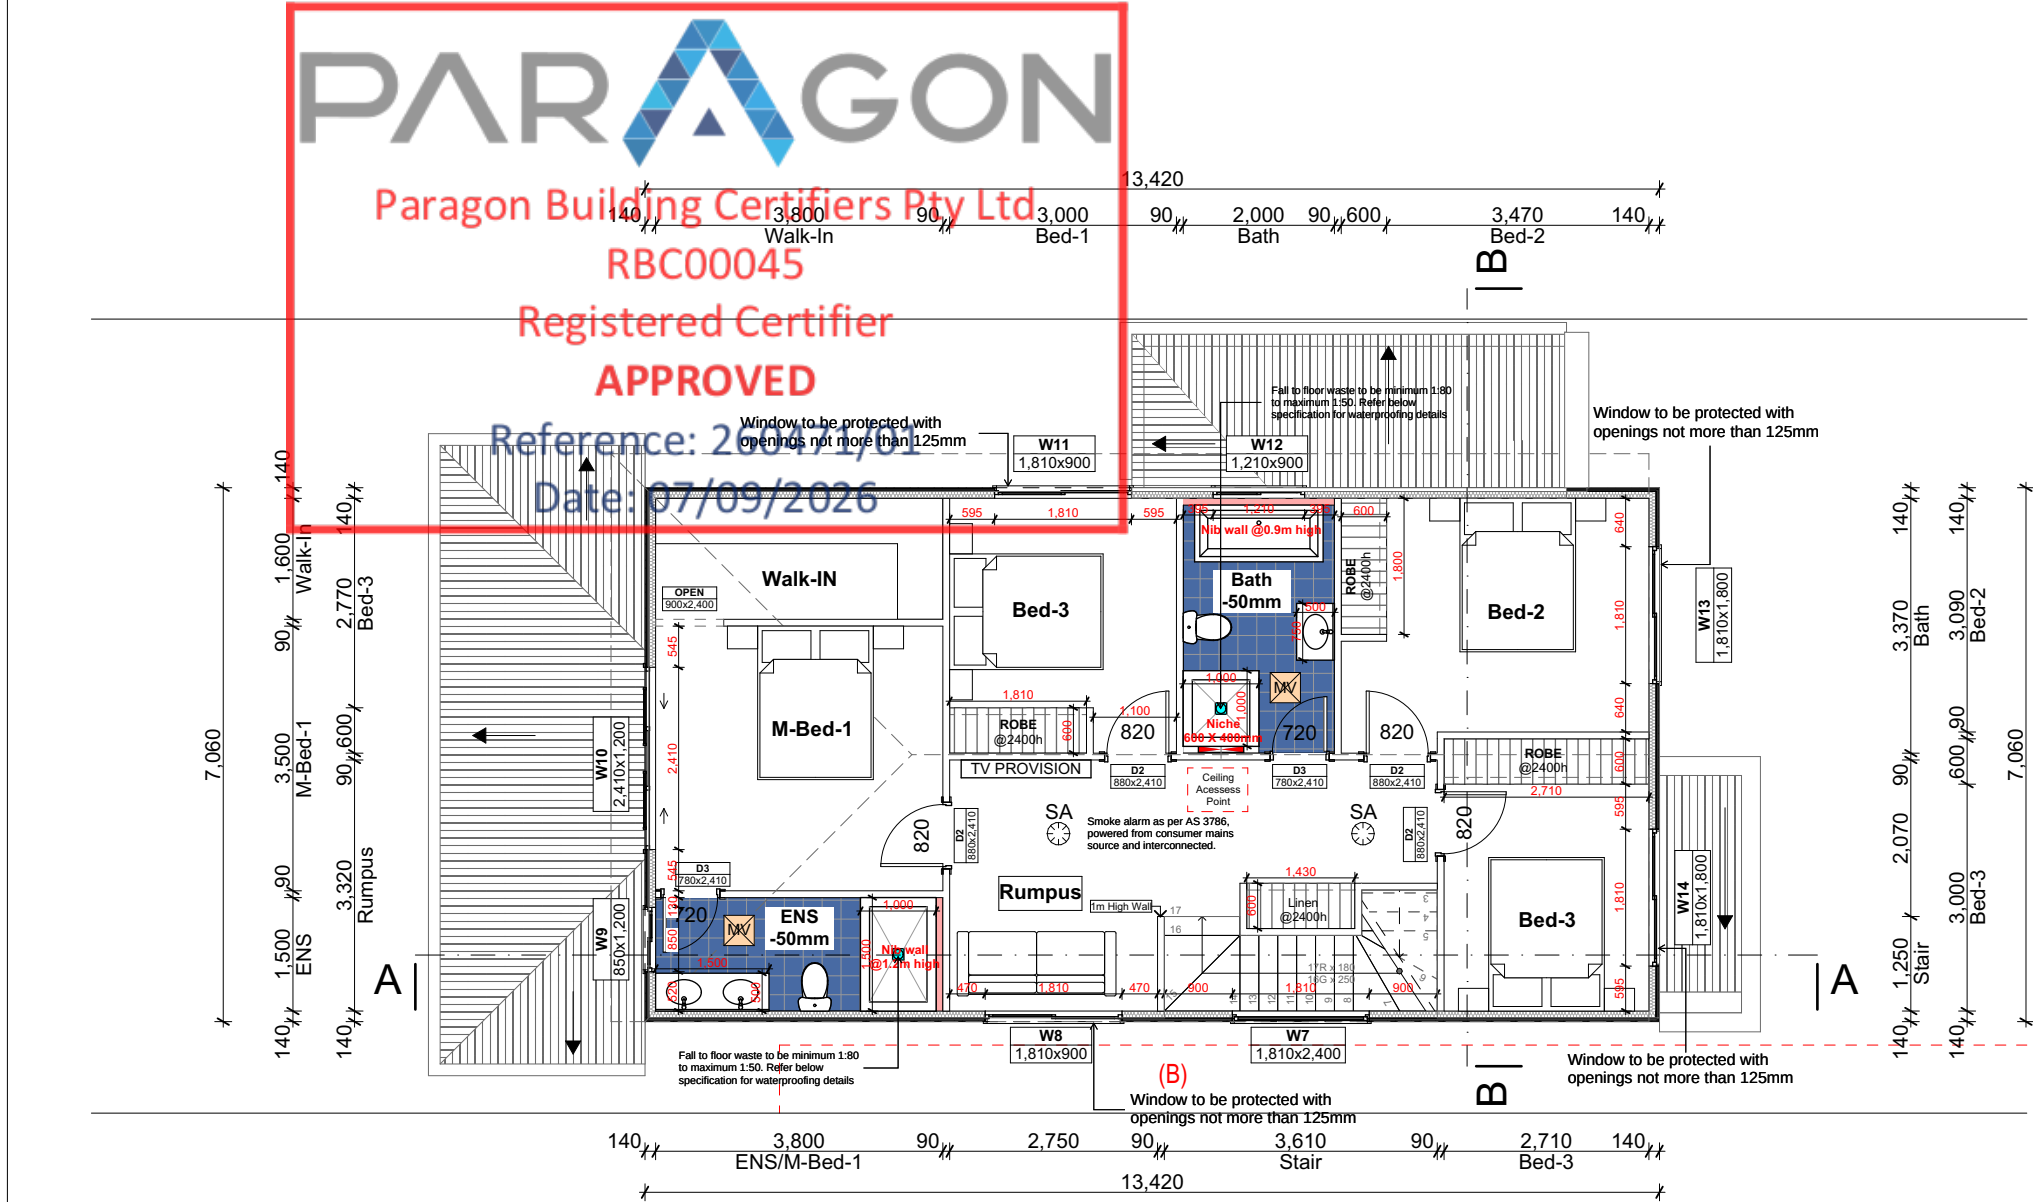

2. First Floor
1:100



NOTE
The Builder shall check all dimensions and levels on site prior to construction. Notify any errors, discrepancies or omissions to the building designer. Refer to written dimensions only. Do not scale drawings. Drawings shall not be used for construction purposes until issued for construction. This drawing reflects a design by Innovative Eco Designs and is to be used only for work when authorised in writing by Innovative Eco Designs.

All boundaries and contours are subject to survey drawing. All levels to Australian Height Data. It is the contractors responsibility to confirm all measurements on site and locations of any services prior to work on site.

All documents here within are subject to Australian Copyright Laws.



**INNOVATIVE
ECO DESIGNS**
Your Home Your Style


37604191460 **ABN**
(02) 8710 3852

SUITE 7, 4-10 SELEMS PDE
REVESBY, NSW, 2212
design@iedesigns.com.au
www.iedesigns.com.au



**ACCREDITED
BUILDING DESIGNER**

B	21-08-2026	Issue for CDC
A	02/08/2026	Issue for CDC

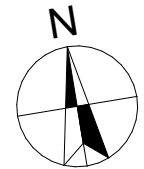

DRAWING : **First Floor Plan**

CLIENT : **Sandstone Constructions Pty Ltd**

PROJECT : **PROPOSED DOUBLE STOREY DWELLING**
#7,Dalgal Street,Austral
Lot-612 D.P 1295393

DRAWN BY: NB	DATE : 21-08-2026	PROJECT NO. 2606 920
SCALE: 1:100	APPLICATION : CDC	ISSUE B
PAGE SIZE A3	PAGE NO: 10	

Waterproofing work to be as per Part 10.2 of the ABCB Housing Provisions Standard 2022

As per 88b, condition no.13 point 4 no building shall be erected or permitted to remain erected on any lot burdened having roof other than Clay tiles, Cement tiles, Slate or non reflective surface corrugated iron. All roofing materials shall be black or shades of grey or natural colours only.

As per section 88b restriction number 11, the lots hereby burdened must be maintained as an Asset Protection Zone (Inner Protection Area) in accordance with Section A4.1.1 of 'Planning for Bushfire Protection 2019' and the NSW Rural Fire Services document 'Standards for Asset Protection Zones.'

PARAGON

Paragon Building Certifiers Pty Ltd


RBC00045

Registered Certifier

APPROVED

Reference: 260471/01

Date: 07/09/2026

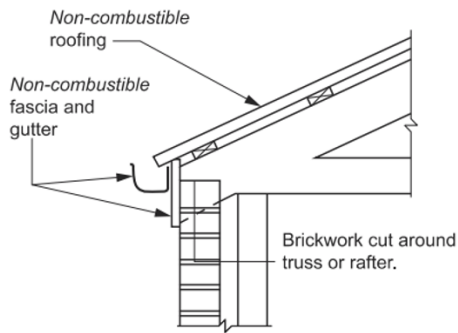

(b) Gutter on face of wall


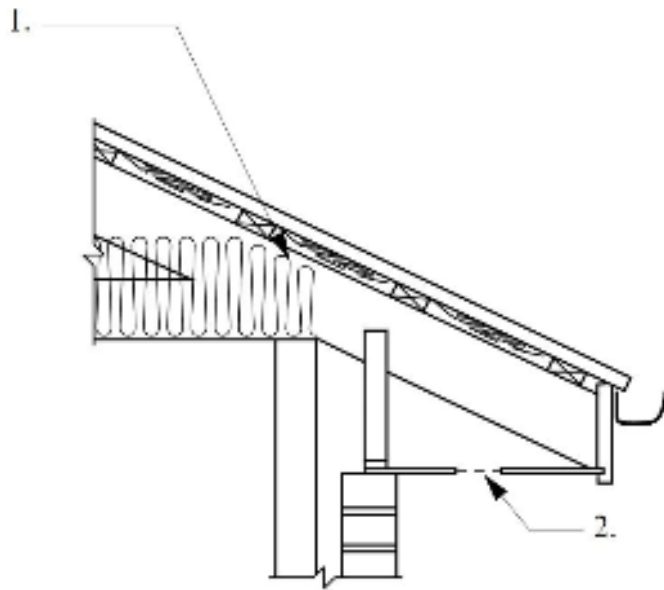


Figure Notes
1. Min 20 mm gap maintained between insulation and sarking
2. Eave ventilation opening in accordance with Table 10.8.3.

Figure 7.2.3: Minimum pitch requirements for metal roofing profiles

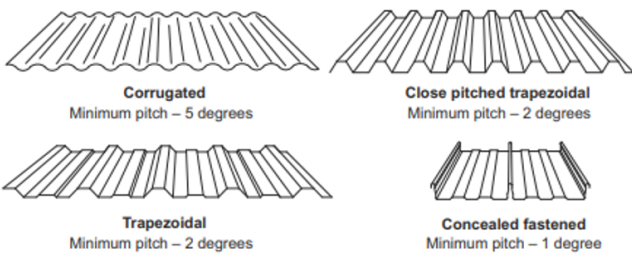

VENTILATION OF ROOF SPACES
ROOF SPACE AS PER 10.8.3 1(a) & 1(b)
(i) VENTILATED TO OUTDOOR AIR THROUGH EVENLY DISTRIBUTED OPENINGS IN ACCORDANCE WITH TABLE 10.8.3, OR

TABLE 10.8.3: ROOF SPACE VENTILATION REQUIREMENTS

ROOF PITCH	VENTILATION OPENINGS
< 10°	25,000 MM2/M PROVIDED AT EACH OF TWO OPPOSING ENDS


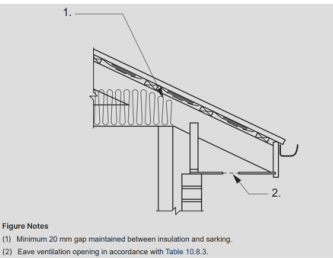


Figure Notes
(1) Minimum 20 mm gap maintained between insulation and sarking.
(2) Eave ventilation opening in accordance with Table 10.8.3.

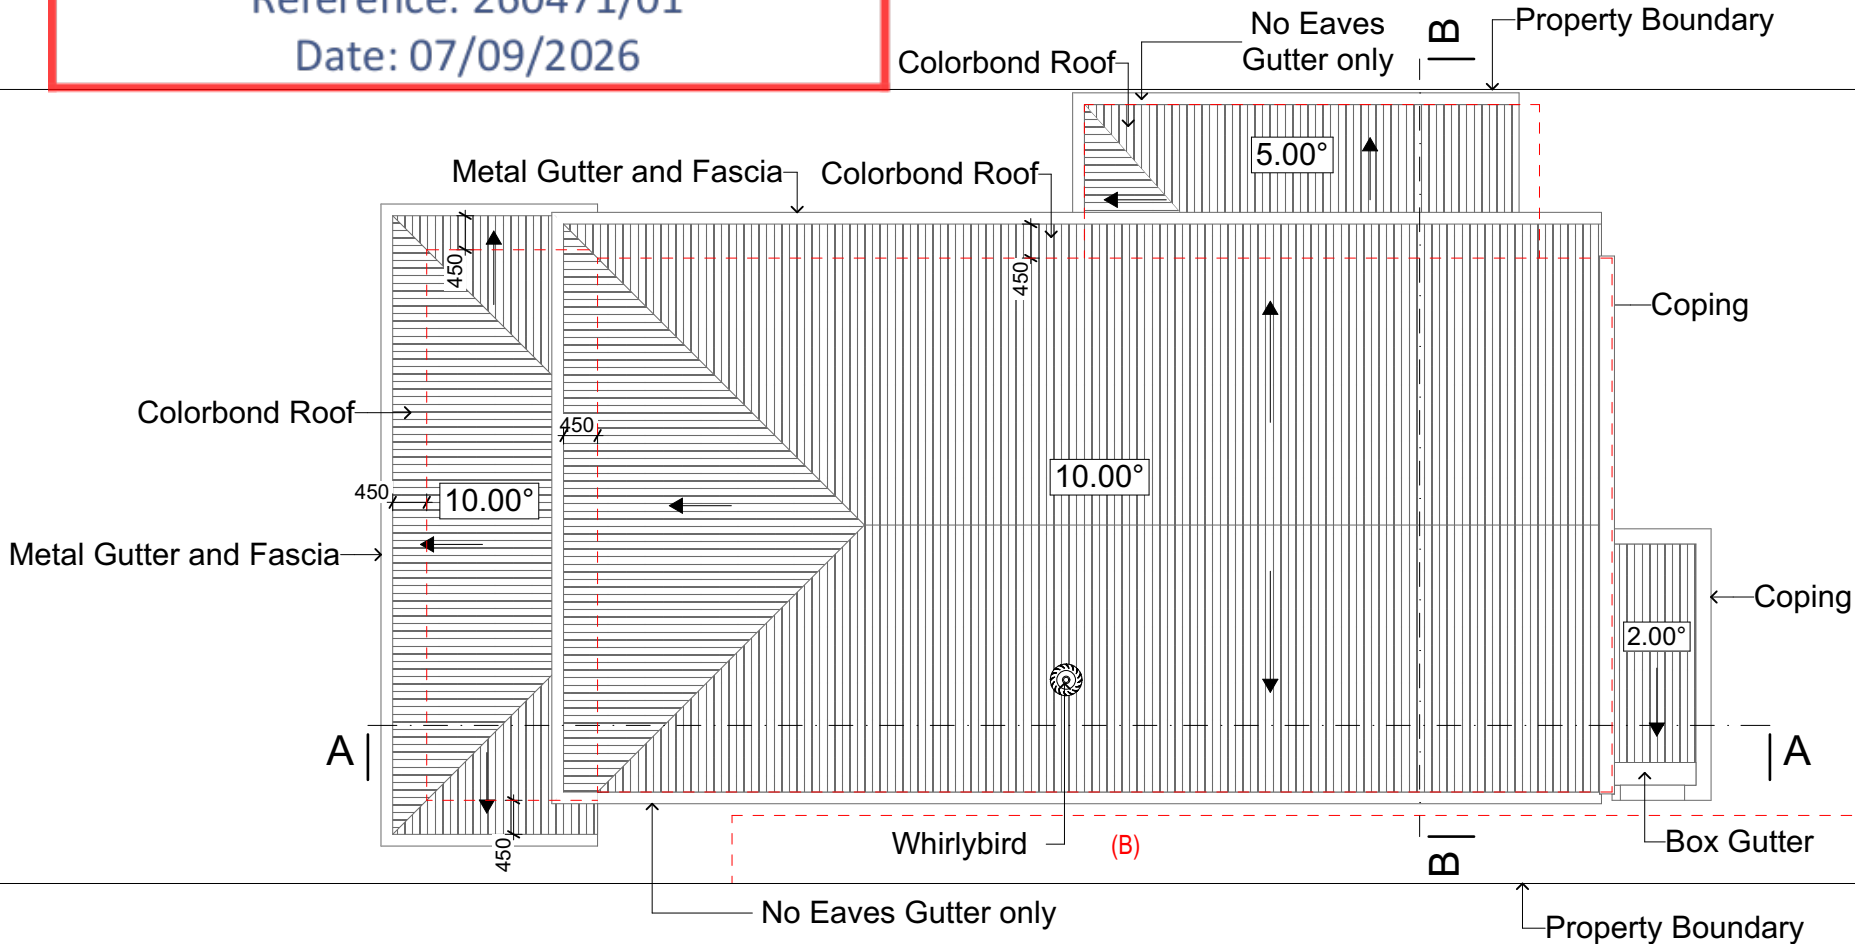

3. Roof
1:100

BEFORE
YOU DIG

www.byda.com.au

Zero Damage - Zero Harm

NOTE
The Builder shall check all dimensions and levels on site prior to construction. Notify any errors, discrepancies or omissions to the building designer. Refer to written dimensions only. Do not scale drawings. Drawings shall not be used for construction purposes until issued for construction. This drawing reflects a design by Innovative Eco Designs and is to be used only for work when authorised in writing by Innovative Eco Designs.

All boundaries and contours are subject to survey drawing. All levels to Australian Height Data. It is the contractors responsibility to confirm all measurements on site and locations of any services prior to work on site.

All documents here within are subject to Australian Copyright Laws.


INNOVATIVE
ECO DESIGNS

Your Home Your Style

37604191460 ABN
(02) 8710 3852
SUITE 7, 4-10 SELEMS PDE
REVESBY, NSW, 2212
design@iedesigns.com.au
www.iedesigns.com.au

ACCREDITED
BUILDING DESIGNER

B	21-08-2026	Issue for CDC
A	02/08/2026	Issue for CDC

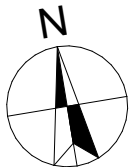


DRAWING : **Roof Plan**
CLIENT : **Sandstone Constructions Pty Ltd**
PROJECT : **PROPOSED DOUBLE STOREY DWELLING**
#7,Dalgal Street,Austral
Lot-612 D.P 1295393

DRAWN BY: NB	DATE : 21-08-2026	PROJECT NO. 2606 920
SCALE: 1:100	APPLICATION : CDC	ISSUE B
PAGE SIZE A3	PAGE NO: 11	

As per 88b, condition no.13 point 4 no building shall be erected or permitted to remain erected on any lot burdened having roof other than Clay tiles, Cement tiles, Slate or non reflective surface corrugated iron. All roofing materials shall be black or shades of grey or natural colours only.

As per section 88b restriction number 11, the lots hereby burdened must be maintained as an Asset Protection Zone (Inner Protection Area) in accordance with Section A4.1.1 of 'Planning for Bushfire Protection 2019' and the NSW Rural Fire Services document 'Standards for Asset Protection Zones.

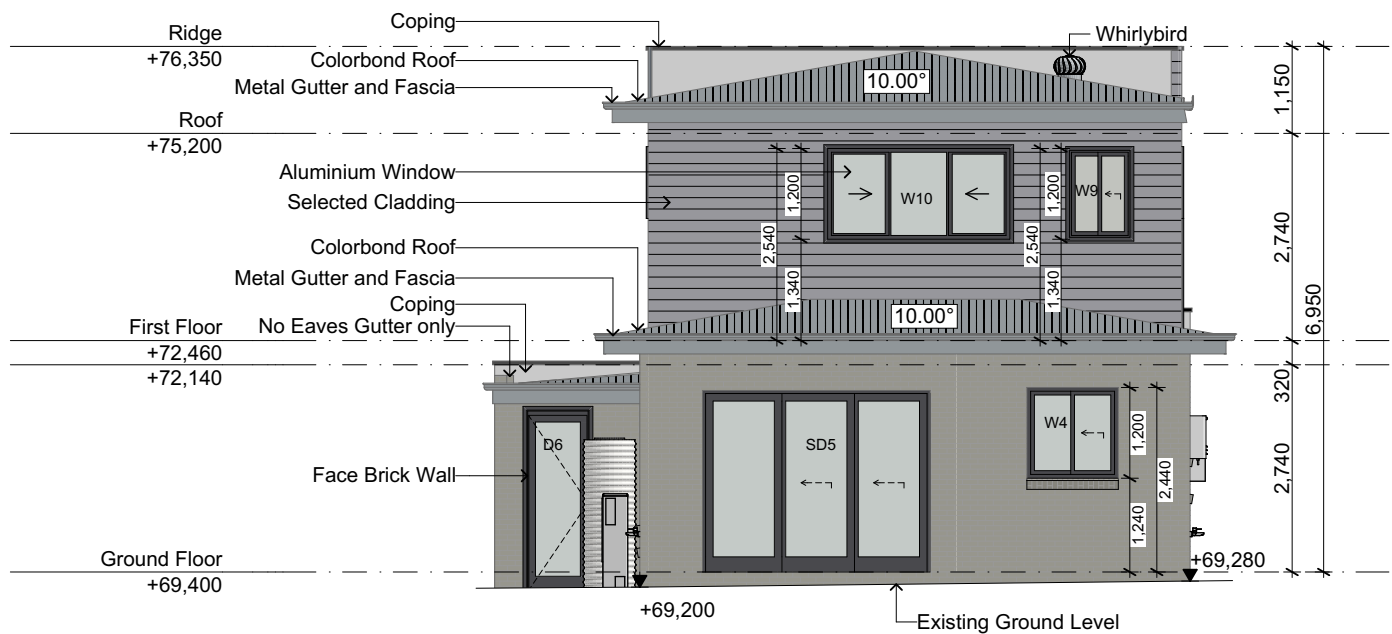

NOTE
The Builder shall check all dimensions and levels on site prior to construction. Notify any errors, discrepancies or omissions to the building designer. Refer to written dimensions only. Do not scale drawings. Drawings shall not be used for construction purposes until issued for construction. This drawing reflects a design by Innovative Eco Designs and is to be used only for work when authorised in writing by Innovative Eco Designs.

All boundaries and contours are subject to survey drawing. All levels to Australian Height Data. It is the contractors responsibility to confirm all measurements on site and locations of any services prior to work on site.

All documents here within are subject to Australian Copyright Laws.



37604191460 ABN
(02) 8710 3852
SUITE 7, 4-10 SELEMS PDE
REVESBY, NSW, 2212
design@iedesigns.com.au
www.iedesigns.com.au



B	21-08-2026	Issue for CDC
A	02/08/2026	Issue for CDC

DRAWING : **Elevation**

CLIENT : **Sandstone Constructions Pty Ltd**

PROJECT : **PROPOSED DOUBLE STOREY DWELLING**
#7,Dalgat Street,Austral
Lot-612 D.P 1295393

DRAWN BY: NB

SCALE: 1:100

PAGE SIZE A3

DATE : **21-08-2026**

APPLICATION : CDC


PAGE NO: 12

PROJECT NO. **2606 920**


ISSUE **B**

As per 88b, condition no.13 point 4 no building shall be erected or permitted to remain erected on any lot burdened having roof other than Clay tiles, Cement tiles, Slate or non reflective surface corrugated iron. All roofing materials shall be black or shades of grey or natural colours only.

As per section 88b restriction number 11, the lots hereby burdened must be maintained as an Asset Protection Zone (Inner Protection Area) in accordance with Section A4.1.1 of 'Planning for Bushfire Protection 2019' and the NSW Rural Fire Services document 'Standards for Asset Protection Zones.

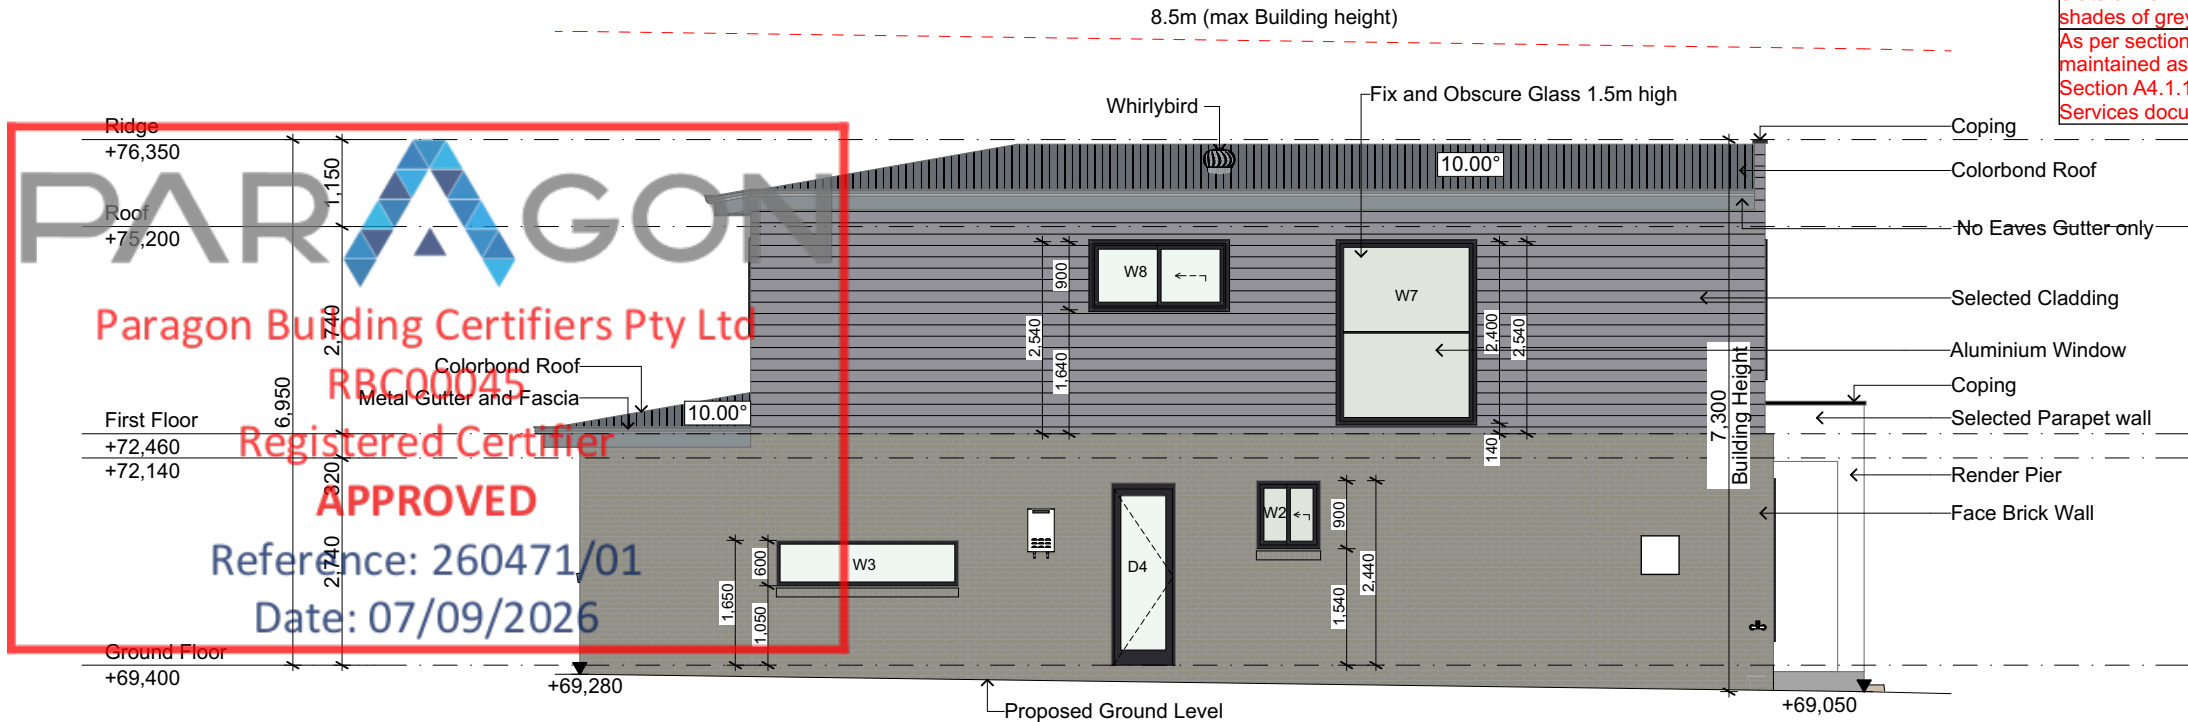

3 South Elevation (Left Side)
1:100

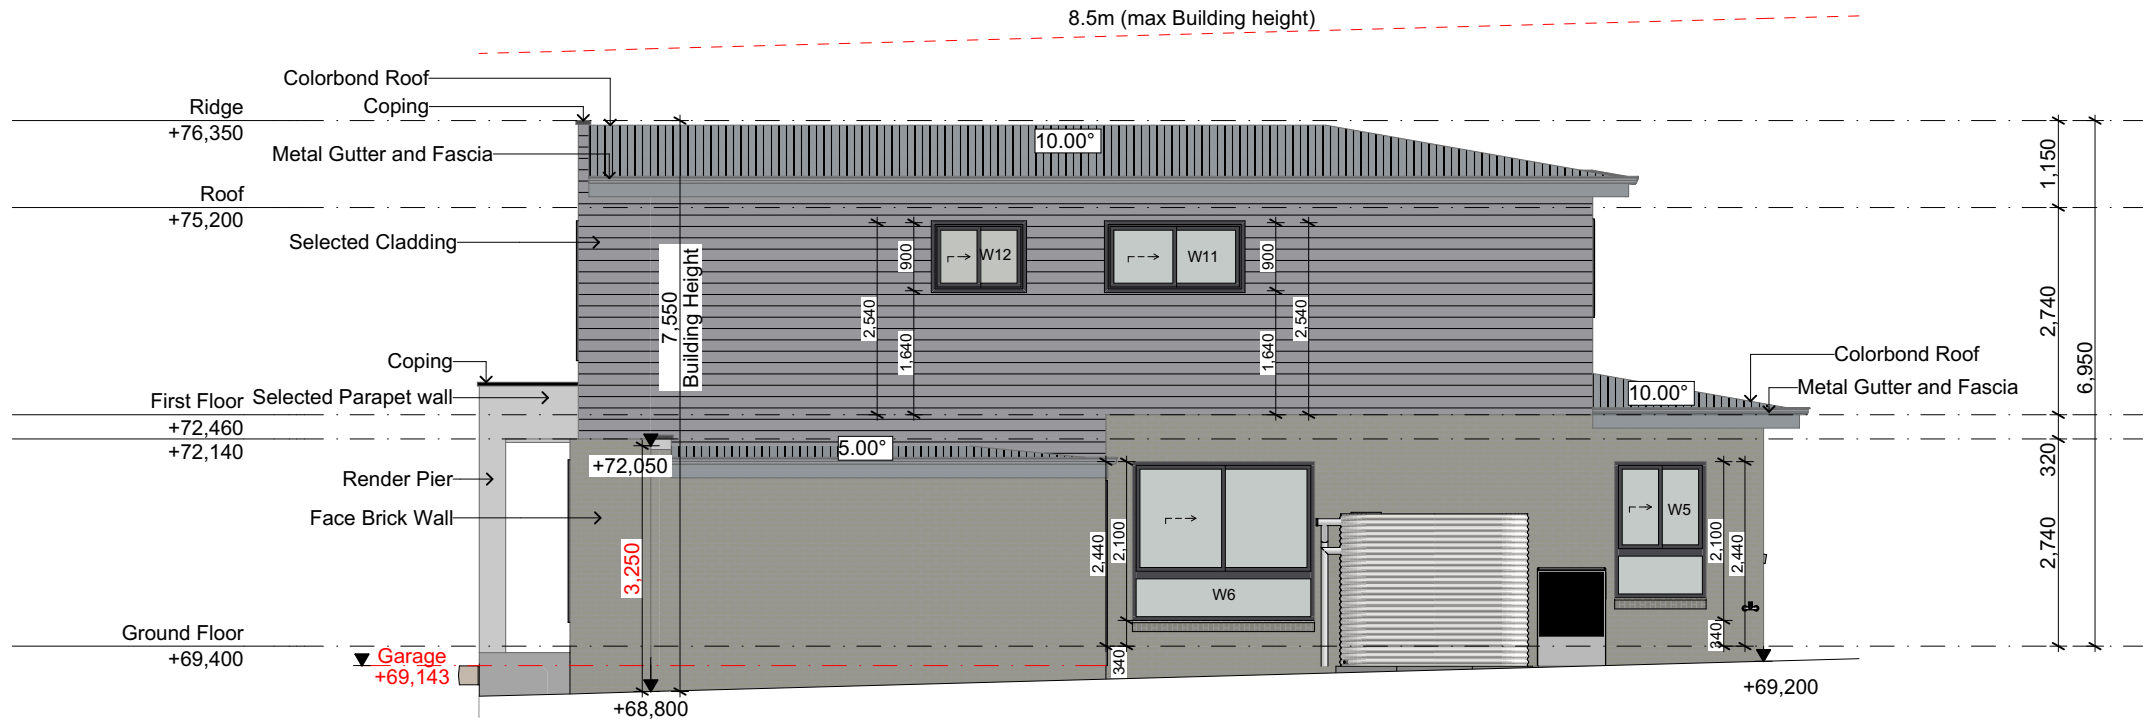

4 North Elevation (Right Side)
1:100



NOTE
The Builder shall check all dimensions and levels on site prior to construction. Notify any errors, discrepancies or omissions to the building designer. Refer to written dimensions only. Do not scale drawings. Drawings shall not be used for construction purposes until issued for construction. This drawing reflects a design by Innovative Eco Designs and is to be used only for work when authorised in writing by Innovative Eco Designs.

All boundaries and contours are subject to survey drawing. All levels to Australian Height Data. It is the contractors responsibility to confirm all measurements on site and locations of any services prior to work on site.

All documents here within are subject to Australian Copyright Laws.



37604191460 ABN
(02) 8710 3852
SUITE 7, 4-10 SELEMS PDE
REVESBY, NSW, 2212
design@iedesigns.com.au
www.iedesigns.com.au





B 21-08-2026 Issue for CDC
A 02/08/2026 Issue for CDC

DRAWING : **Side Elevation**
CLIENT : **Sandstone Constructions Pty Ltd**
PROJECT : **PROPOSED DOUBLE STOREY DWELLING**
#7,Dalgal Street,Austral
Lot-612 D.P 1295393

DRAWN BY: NB
SCALE: 1:100
PAGE SIZE A3
DATE : **21-08-2026**
APPLICATION : CDC
PAGE NO: 13






PROJECT NO. **2606 920**
ISSUE **B**


As per section 88b restriction number 11, the lots hereby burdened must be maintained as an Asset Protection Zone (Inner Protection Area) in accordance with Section A4.1.1 of 'Planning for Bushfire Protection 2019' and the NSW Rural Fire Services document 'Standards for Asset Protection Zones.'

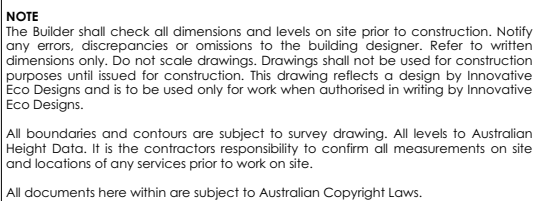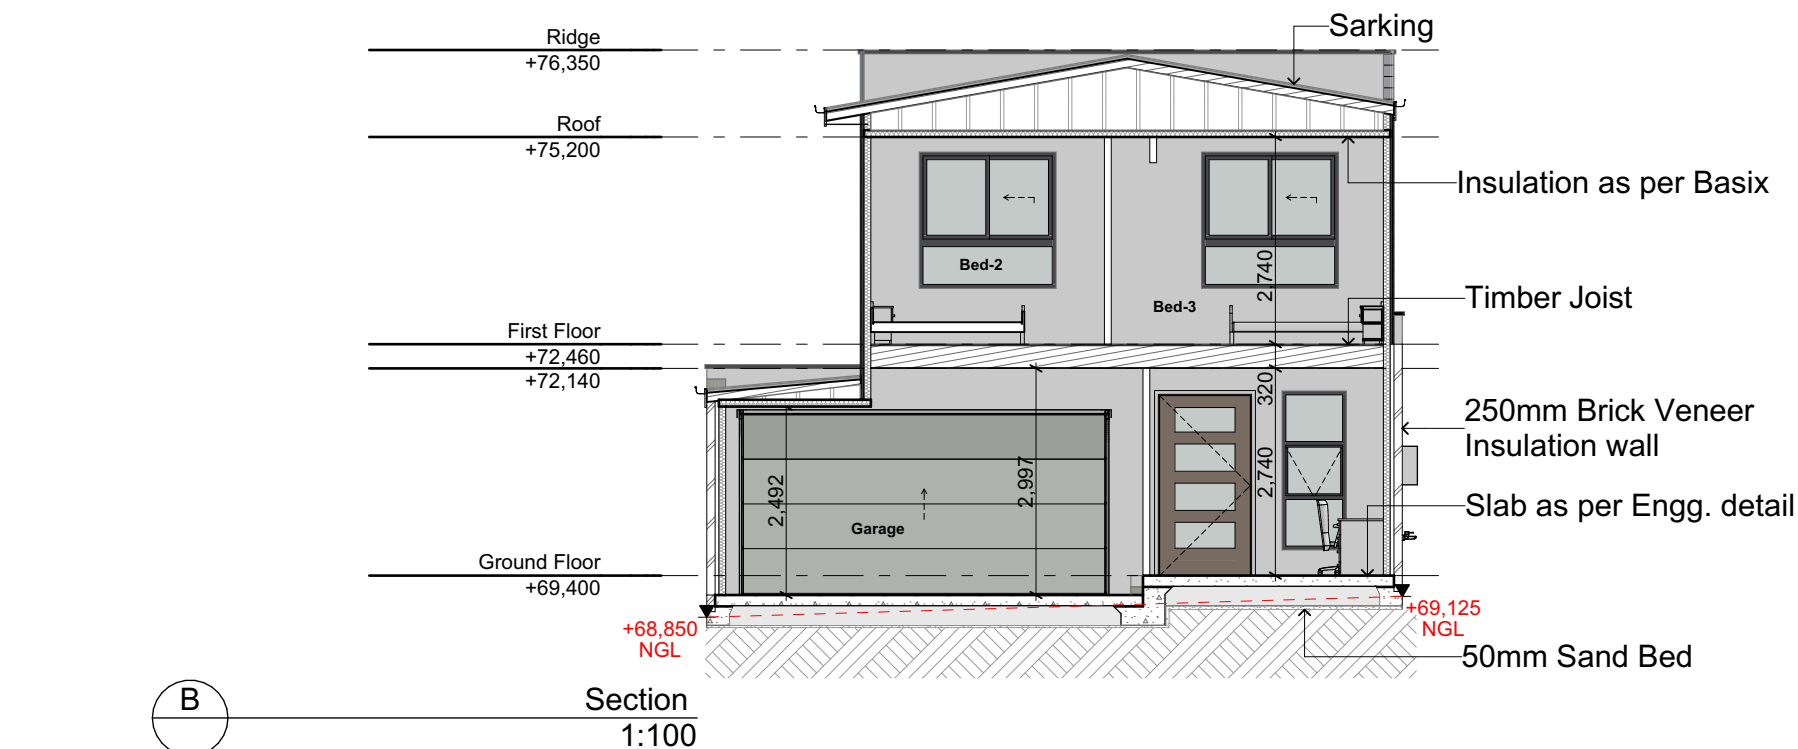

B	21-08-2026	Issue for CDC
A	02/08/2026	Issue for CDC

DRAWING : Section	DRAWN BY: NB	DATE : 21-08-2026	PROJECT NO. 2606 920
CLIENT : Sandstone Constructions Pty Ltd	SCALE: 1:100	APPLICATION : CDC	ISSUE B
PROJECT : PROPOSED DOUBLE STOREY DWELLING #7,Dalgai Street,Austral Lot-612 D.P 1295393	PAGE SIZE A3	PAGE NO: 14	

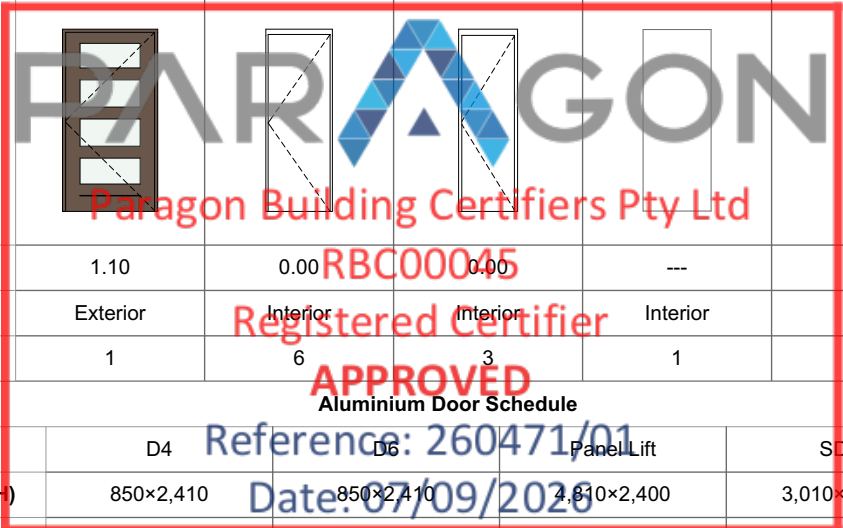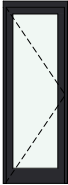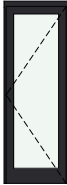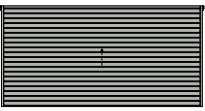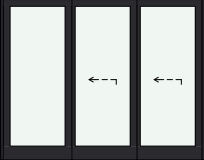Door Schedule					
ID	D1	D2	D3	OPEN	
Wallhole Dimensions(W x H)	1,260×2,410	880×2,410	780×2,410	900×2,400	
Leaf Dimensions	1,200×2,380	820×2,340	720×2,340	---	
Elevation					
Total Glazed Area SQM	1.10	0.00	0.00	---	1.10
Position	Exterior	Interior	Interior	Interior	
Quantity	1	6	3	1	11
Aluminium Door Schedule					
ID	D4	D6	Panel Lift	SD5	
Frame Dimensions (W X H)	850×2,410	850×2,410	4,810×2,400	3,010×2,400	
Elevation					
Total Glazed Area SQM	1.21	1.21	1.41	4.80	8.63
Glazed Area SQM	---	---	---	---	0.00
Position	Exterior	Exterior	Exterior	Exterior	
Quantity	1	1	1	1	4

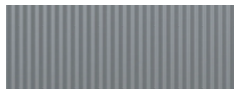SCHEDULE OF FINISHES		
Element	SPECIFICATION	COLOUR
Walls	PGH Botanicals Sage	
F.F Walls	Cladding-Grid	
Roof	Colorbond-Bluegum	
Gutter	Bluegum	
Fascia	Bluegum	
Window	Black	
Garage Door	Ironstone	
As per 88b, condition no.13 point 4 no building shall be erected or permitted to remain erected on any lot burdened having roof other than Clay tiles, Cement tiles, Slate or non reflective surface corrugated iron. All roofing materials shall be black or shades of grey or natural colours only.		
As per section 88b restriction number 11, the lots hereby burdened must be maintained as an Asset Protection Zone (Inner Protection Area) in accordance with Section A4.1.1 of 'Planning for Bushfire Protection 2019" and the NSW Rural Fire Services document 'Standards for Asset Protection Zones.		



NOTE
The Builder shall check all dimensions and levels on site prior to construction. Notify any errors, discrepancies or omissions to the building designer. Refer to written dimensions only. Do not scale drawings. Drawings shall not be used for construction purposes until issued for construction. This drawing reflects a design by Innovative Eco Designs and is to be used only for work when authorised in writing by Innovative Eco Designs.

All boundaries and contours are subject to survey drawing. All levels to Australian Height Data. It is the contractors responsibility to confirm all measurements on site and locations of any services prior to work on site.

All documents here within are subject to Australian Copyright Laws.



37604191460 **ABN**
(02) 8710 3852
SUITE 7, 4-10 SELEMS PDE
REVESBY, NSW, 2212
design@iedesigns.com.au
www.iedesigns.com.au




B	21-08-2026	Issue for CDC
A	02/08/2026	Issue for CDC




DRAWING : **Door Schedule & SOF**

CLIENT : **Sandstone Constructions Pty Ltd**

PROJECT : **PROPOSED DOUBLE STOREY DWELLING**
#7,Dalgat Street,Austral
Lot-612 D.P 1295393

DRAWN BY: NB	DATE : 21-08-2026	PROJECT NO. 2606 920
SCALE:	APPLICATION : CDC	ISSUE B
PAGE SIZE A3	PAGE NO: 15	

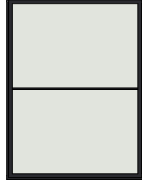Window Schedule									
ID	W1	W2	W3	W4	W5	W6	W7	W8	W9
Frame Dimensions	850×2,100	850×900	2,410×600	1,210×1,200	1,210×1,800	2,410×2,100	1,810×2,400	1,810×900	850×1,200
Elevation									
Glass	Glass - Clear	Glass - Obscure	Glass - Clear	Glass - Clear	Glass - Clear	Glass - Clear	Glass - Obscure	Glass - Clear	Glass - Obscure
Glazed Area SQM	1.36	0.42	1.16	0.96	1.52	3.96	3.70	1.09	0.60
Glazed Area SQM	---	---	---	---	---	---	---	---	---
Quantity	1	1	1	1	1	1	1	1	1

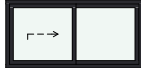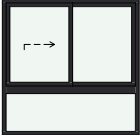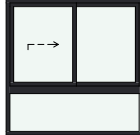Window Schedule						
ID	W10	W11	W12	W13	W14	
Frame Dimensions	2,410×1,200	1,810×900	1,210×900	1,810×1,800	1,810×1,800	
Elevation						
Glass	Glass - Clear	Glass - Clear	Glass - Obscure	Glass - Clear	Glass - Clear	
Glazed Area SQM	0.00	1.09	0.67	2.42	2.42	21.37
Glazed Area SQM	2.25	---	---	---	---	2.25
Quantity	1	1	1	1	1	14

NOTE:
- TO BE CHECKED AND CONFIRMED BY BUILDER ON SITE BEFORE PLACING ORDER.
-FALL PREVENTION FROM WINDOWS
-WINDOWS TO BE MANUFACTURED IN ACCORDANCE WITH REQUIREMENTS OF NCC 2022 vol. 2 part 11.3.7
1- If Opening withing 1700mm above the floor; and climable elements between 150 and 750 mM above the floor, opening must be permanently restricted to 125mm; or fitted withn a non-removable robust screen.
2-If opening between 865 and 1700mm above the floor; and no climable elements between 150 and 760mm bove the floor, opening must be restricted to 125mm; or fitted with a removable robust screen.
3- If opening between 865 of the floor; and climable elements between 150 and 760mm above the floor;or fitted with a non-removable robust screen.
4-If no opening within 1700mm of the floor. No restrictions apply.

Part 11.3.7 Protection of openable windows - bedrooms
(1) A window opening in a bedroom must be provided with protection, where the floor below the window is 2 m or more above the surface beneath.
(2) Where the lowest level of the window opening covered by (1) is less than 1.7 m above the floor, the window opening must comply with the following:
(a) The openable portion of the window must be protected with-
(i) a device capable of restricting the window opening; or
(ii) a screen with secure fittings.
(b) A device or screen required by (a) must-
(i) not permit a 125 mm sphere to pass through the window opening or screen; and
(ii) resist an outward horizontal action of 250 N against the-
(A) window restrained by a device; or
(B) screen protecting the opening; and
(iii) have a child resistant release mechanism if the screen or device is able to be removed, unlocked or overridden.
(3) Where a device or screen provided in accordance with (2)(a) is able to be removed, unlocked or overridden, a barrier with a height not less than 865 mm above the floor is required to the openable window in addition to window protection.
(4) A barrier covered by (3) must not-
(a) permit a 125 mm sphere to pass through it; and
(b) have any horizontal or near horizontal elements between 150 mm and 760 mm above the floor that facilitate climbing.

11.3.8 Protection of openable windows - rooms other than bedrooms
(1) A window opening in a room other than a bedroom must be provided with protection where the floor below the window is 4 m or more above the surface beneath.
(2) The openable part of the window covered by (a) must be protected with a barrier with a height of not less than 865mm above the floor.
(3) A barrier required by (b) must not-
(a) permit a 125 mm sphere to pass through it; and
(b) have any horizontal or near horizontal elements between 150 mm and 760 mm above the floor that facilitate climbing.

As per 88b, condition no.13 point 4 no building shall be erected or permitted to remain erected on any lot burdened having roof other than Clay tiles, Cement tiles, Slate or non reflective surface corrugated iron. All roofing materials shall be black or shades of grey or natural colours only.

As per section 88b restriction number 11, the lots hereby burdened must be maintained as an Asset Protection Zone (Inner Protection Area) in accordance with Section A4.1.1 of 'Planning for Bushfire Protection 2019" and the NSW Rural Fire Services document 'Standards for Asset Protection Zones.



NOTE
The Builder shall check all dimensions and levels on site prior to construction. Notify any errors, discrepancies or omissions to the building designer. Refer to written dimensions only. Do not scale drawings. Drawings shall not be used for construction purposes until issued for construction. This drawing reflects a design by Innovative Eco Designs and is to be used only for work when authorised in writing by Innovative Eco Designs.

All boundaries and contours are subject to survey drawing. All levels to Australian Height Data. It is the contractors responsibility to confirm all measurements on site and locations of any services prior to work on site.

All documents here within are subject to Australian Copyright Laws.



37604191460 **ABN**
(02) 8710 3852
SUITE 7, 4-10 SELEMS PDE
REVESBY, NSW,2212
design@iedesigns.com.au
www.iedesigns.com.au



B	21-08-2026	Issue for CDC
A	02/08/2026	Issue for CDC

DRAWING : **Window Schedule**

CLIENT : **Sandstone Constructions Pty Ltd**

PROJECT : **PROPOSED DOUBLE STOREY DWELLING**
#7,Dalgai Street,Austral
Lot-612 D.P 1295393

DRAWN BY: NB	DATE : 21-08-2026	PROJECT NO. 2606 920
SCALE:	APPLICATION : CDC	ISSUE B
PAGE SIZE A3	PAGE NO: 16	

All Landscape to be done by owner.

LANDSCAPE SCHEDULE

Refrence Image	ABB	NAME	TYPE	HEIGHT	POT. SIZE	QUA.
	(ML)	MELALEUCA LINARIIFOLIA	Tree	8-15m	75LT.	1
	(PC)	PYRUS CALLERYANA (CHANTICLEER)	Tree	5m	45LT.	1
	(BS)	BANKSIA SPINULOSA	Shrub	1-3m	300mm	8
		BUFFALO GRASS	Grass			
		AGGREGATE				

LEGEND

Ref.img	Name
	Tree
	Shrub
	Grass (Landscape Area)
	Aggregate

GE:- GARDEN EDGING AS SELECTED
TREATED PINE SPLITS 90 MM 2.4 MT LENGTH,
FASTENED TO HARWOOD STAKES, MINIMUM DEPTH
IN GROUND OF 300 MM WITH GALVANISED TREATED
PINE SCREWS(SIZE 75 MM X 8G)

LAWN:- BUFFALO WITH SHIRLEYS NO.17 FERTILISER
ALL PLANTS TO HAVE 35 MM OF BARK CHIP MULCH
SPREAD OVER TOP SOIL TURF TO BE WATERED
MORNING AND EVENING FOR A PERIOD OF TWO
WEEKS OR AD NECESSARY.

As per 88b, condition no.13 point 4 no building shall be erected or permitted to remain erected on any lot
burdened having roof other than Clay tiles, Cement tiles, Slate or non reflective surface corrugated iron. All
roofing materials shall be black or shades of grey or natural colours only.

As per section 88b restriction number 11, the lots hereby burdened must be maintained as an Asset
Protection Zone (Inner Protection Area) in accordance with Section A4.1.1 of 'Planning for Bushfire
Protection 2019' and the NSW Rural Fire Services document 'Standards for Asset Protection Zones.



Paragon Building Certifiers Pty Ltd

RBC00045


Registered Certifier

APPROVED

Reference: 260471/01

Date: 07/09/2026

Mail Box
1:20

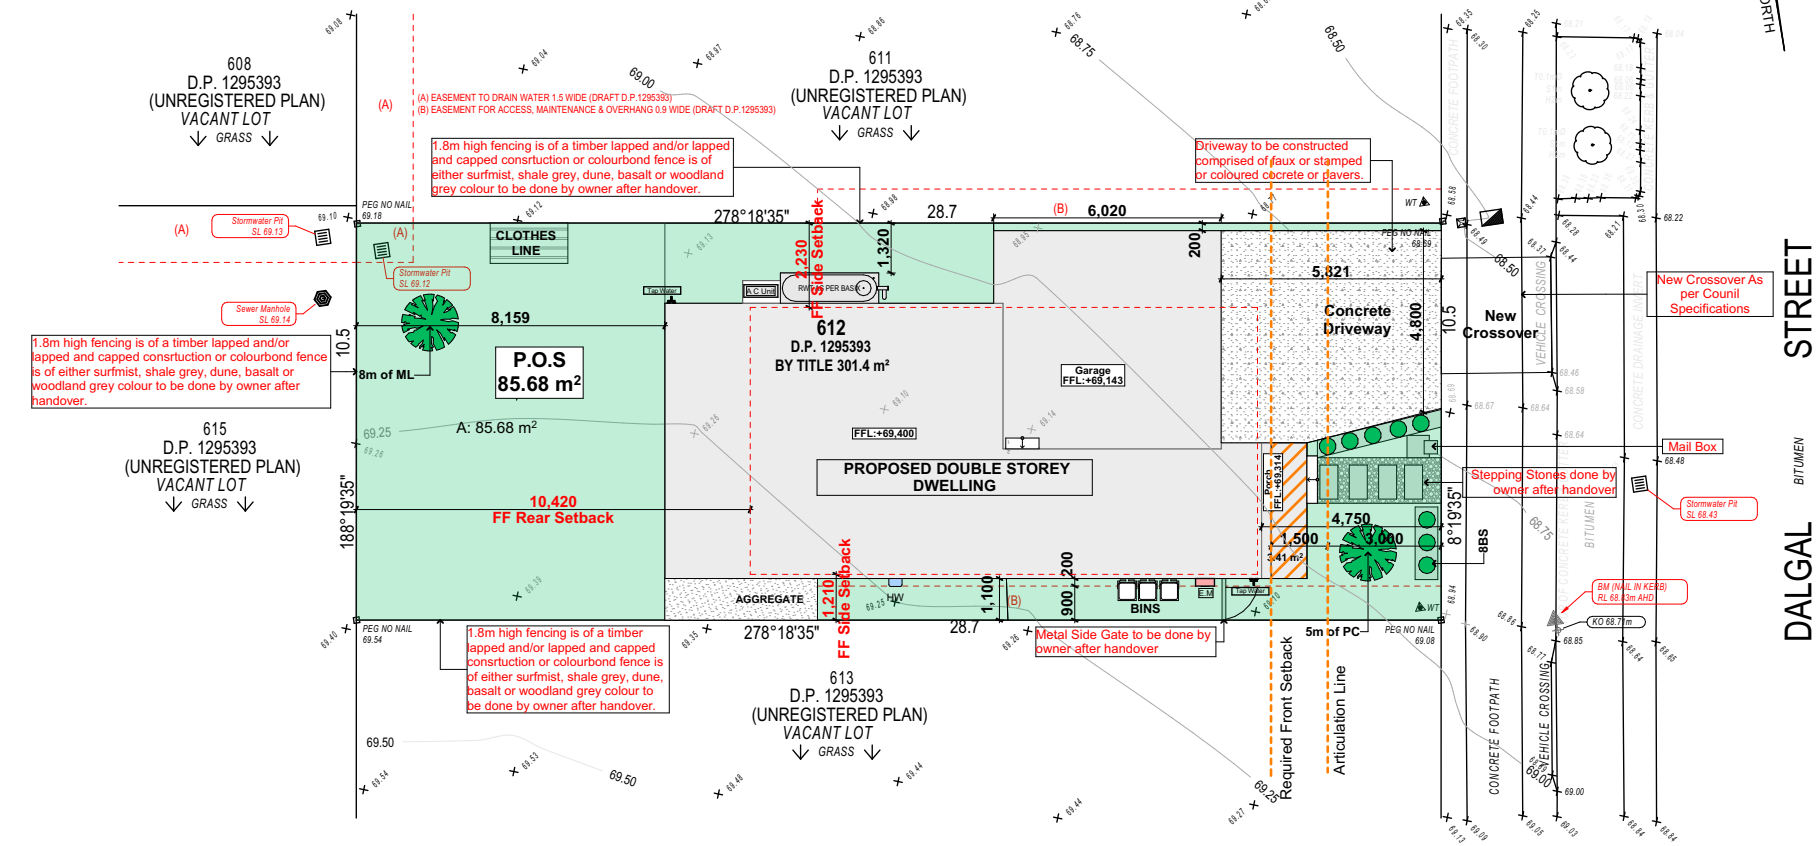

Landscape Plan
1:200

NOTE
The Builder shall check all dimensions and levels on site prior to construction. Notify any errors, discrepancies or omissions to the building designer. Refer to written dimensions only. Do not scale drawings. Drawings shall not be used for construction purposes until issued for construction. This drawing reflects a design by Innovative Eco Designs and is to be used only for work when authorised in writing by Innovative Eco Designs.

All boundaries and contours are subject to survey drawing. All levels to Australian Height Data. It is the contractors responsibility to confirm all measurements on site and locations of any services prior to work on site.


All documents here within are subject to Australian Copyright Laws.



37604191460 ABN
(02) 8710 3852
SUITE 7, 4-10 SELEMS PDE
REVESBY, NSW, 2212
design@iedesigns.com.au
www.iedesigns.com.au






B	21-08-2026	Issue for CDC
A	02/08/2026	Issue for CDC

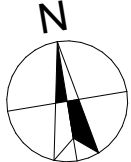

DRAWING : **Landscape Plan**
CLIENT : **Sandstone Constructions Pty Ltd**
PROJECT : **PROPOSED DOUBLE STOREY DWELLING**
#7,Dalgai Street,Austral
Lot-612 D.P 1295393

DRAWN BY: NB
SCALE: 1:200
PAGE SIZE A3
DATE : 21-08-2026
APPLICATION : CDC
PAGE NO: 17
PROJECT NO. 2606 920
ISSUE B

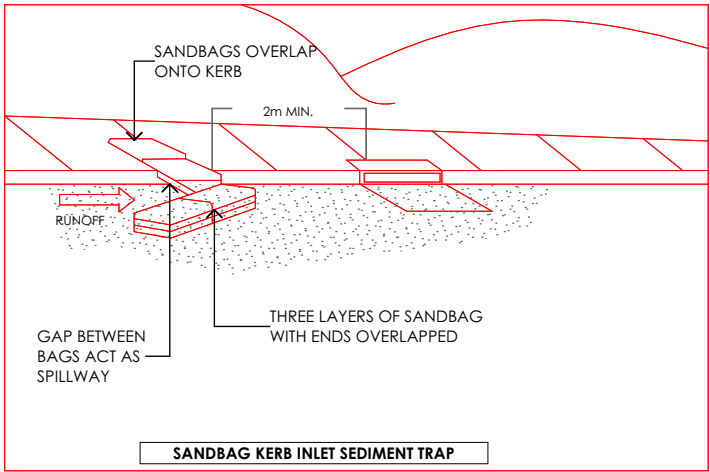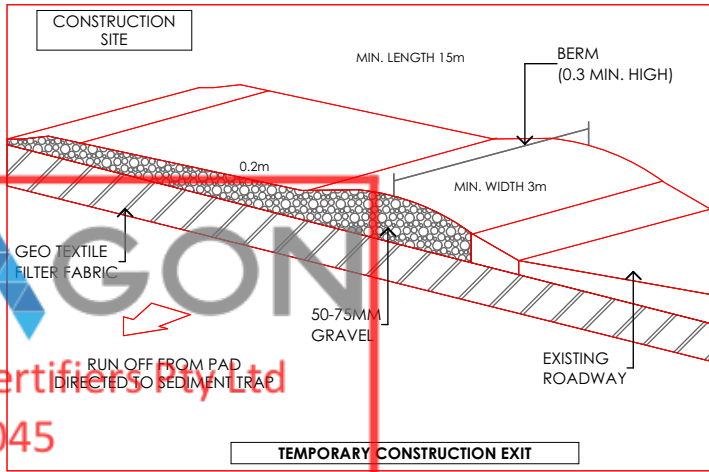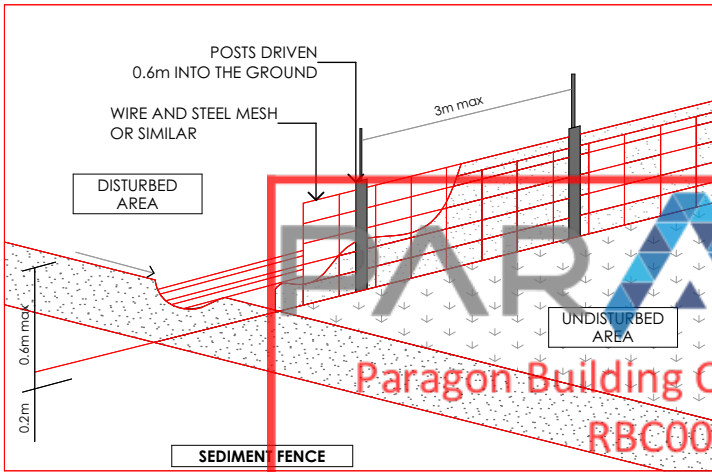

SEDIMENT CONTROL NOTES

1. ALL EROSION AND SEDIMENTATION CONTROL MEASURES, INCLUDING REVEGETATION AND STORAGE OF SOIL AND TOPSOIL, SHALL BE IMPLEMENTED TO THE STANDARDS OF THE SOIL CONSERVATION OF NSW.
2. ALL DRAINAGE WORKS SHALL BE CONSTRUCTED AND STABILIZED AS EARLY AS POSSIBLE DURING DEVELOPMENT.
3. SEDIMENT TRAPS SHALL BE CONSTRUCTED AROUND ALL INLET PITS, CONSISTING OF 300mm WIDE x 300mm DEEP TRENCH.
4. ALL SEDIMENT BASINS AND TRAPS SHALL BE CLEANED WHEN THE STRUCTURES AREA MAXIMUM OF 60% FULL OF SOIL MATERIALS, INCLUDING THE MAINTENANCE PERIOD.
5. ALL DISTURBED AREAS SHALL BE REVEGITATED AS SOON AS THE RELEVANT WORKS ARE COMPLETED.
6. SOIL AND TOPSOIL STOCKPILES SHALL BE LOCATED AWAY FROM DRAINAGE LINES AND AREA WHERE WATER MAY CONCENTRATE.
7. FILTER SHALL BE CONSTRUCTED BY STRETCHING A FILTER FABRIC(PROPEX OR APPROVED EQUIVALENT BETWEEN POST AT 3.0m CENTRES. FABRIC SHALL BE BURIED 150mm ALONG ITS LOWER.

Paragon Building Certifiers Pty Ltd
RBC00045
Registered Certifier
APPROVED
Reference: 260471/01
Date: 07/09/2026


TOPSOIL SHALL BE STRIPPED AND STOCKPILED OUTSIDE HAZARD AREAS SUCH AS DRAINAGE LINES. THIS TOPSOIL IS TO BE RE-SPREAD LATER ON AREAS TO BE REVEGETATED AND STABILISED ONLY. (i.e ALL FOOT-PATHS, BATTERS, SITE, REGRADING AREAS, DRAINAGE RESERVES AND CHANNELS). TOP SOIL SHALL NOT BE SPREAD ON ANY OTHER AREAS SPECIFICALLY INSTRUCTED BY THE SUPERINTENDENT. IF THEY ARE TO REMAIN FOR LONGER THAN ONE MONTH STOCKPILES SHALL BE PROTECTED FROM EROSION BY COVERING THEM WITH A MULCH AND HYDROSEEDING AND, IF NECESSARY, BY LOCATING BANKS OR DRAINS UPSLOPE TO DIVERT THE RUNOFF AROUND THEM. IN SOME CIRCUMSTANCES IT MAY BE NECESSARY TO PLACE BANKS OR DRAINS DOWN STREAM OF A STOCKPILE TO RETARD SEDIMENT LADEN RUNOFF. THE CONTRACTOR SHALL REGULARLY MAINTAIN ALL SEDIMENT AND EROSION CONTROL DEVICES AND REMOVE ACCUMULATED SILT FROM SUCH DEVICES BEFORE NO MORE THAN 60% OF THEIR CAPACITY IS LOST. ALL THE SILT REMOVED SHALL BE DISPOSED OF AS DIRECTED BY THE SUPERINTENDENT. (NO SILT SHALL BE PLACED OUTSIDE THE LIMITS OF WORKS). THE PERIOD FOR MAINTAINING THESE DEVICES SHALL BE AT LEAST UNTIL ALL DISTURBED AREAS ARE REVEGETATED AND FURTHER AS MAY BE DIRECTED BY THE SUPERINTENDENT OR COUNCIL

SEDIMENT NOTES

1. CONSTRUCT SEDIMENT FENCE AS CLOSE AS POSSIBLE AND PARALLEL TO THE CONTOURS OF THE SITE.
2. DRIVE 1.5 m LONG STAR PICKETS INTO GROUND Max 3 m Ctrs.
3. DIG A 150 mm DEEP TRENCH ALONG THE UPSLOPE LINE OF THE FENCE FOR THE BOTTOM OF THE FABRIC TO BE ENTRENCHED.
4. BACKFILL TRENCH OVER BASE OF FABRIC.
5. FIX SELF SUPPORTING GEOTEXILE TO UPSLOPE SIDE OF POSTS WITH WIRE TIES OR AS RECOMMENDED BY GEOTEXILE MANUFACTURER.
6. JOIN SECTIONS OF FABRIC AT A SUPPORT POST WITH A Min LAP OF 150 mm.

***THIS DRAWING SHALL BE READ IN CONJUNCTION WITH THE FOLLOWING:**

1-ARCHITECTURAL PLANS
2-CONTOUR AND DETAIL SURVEY

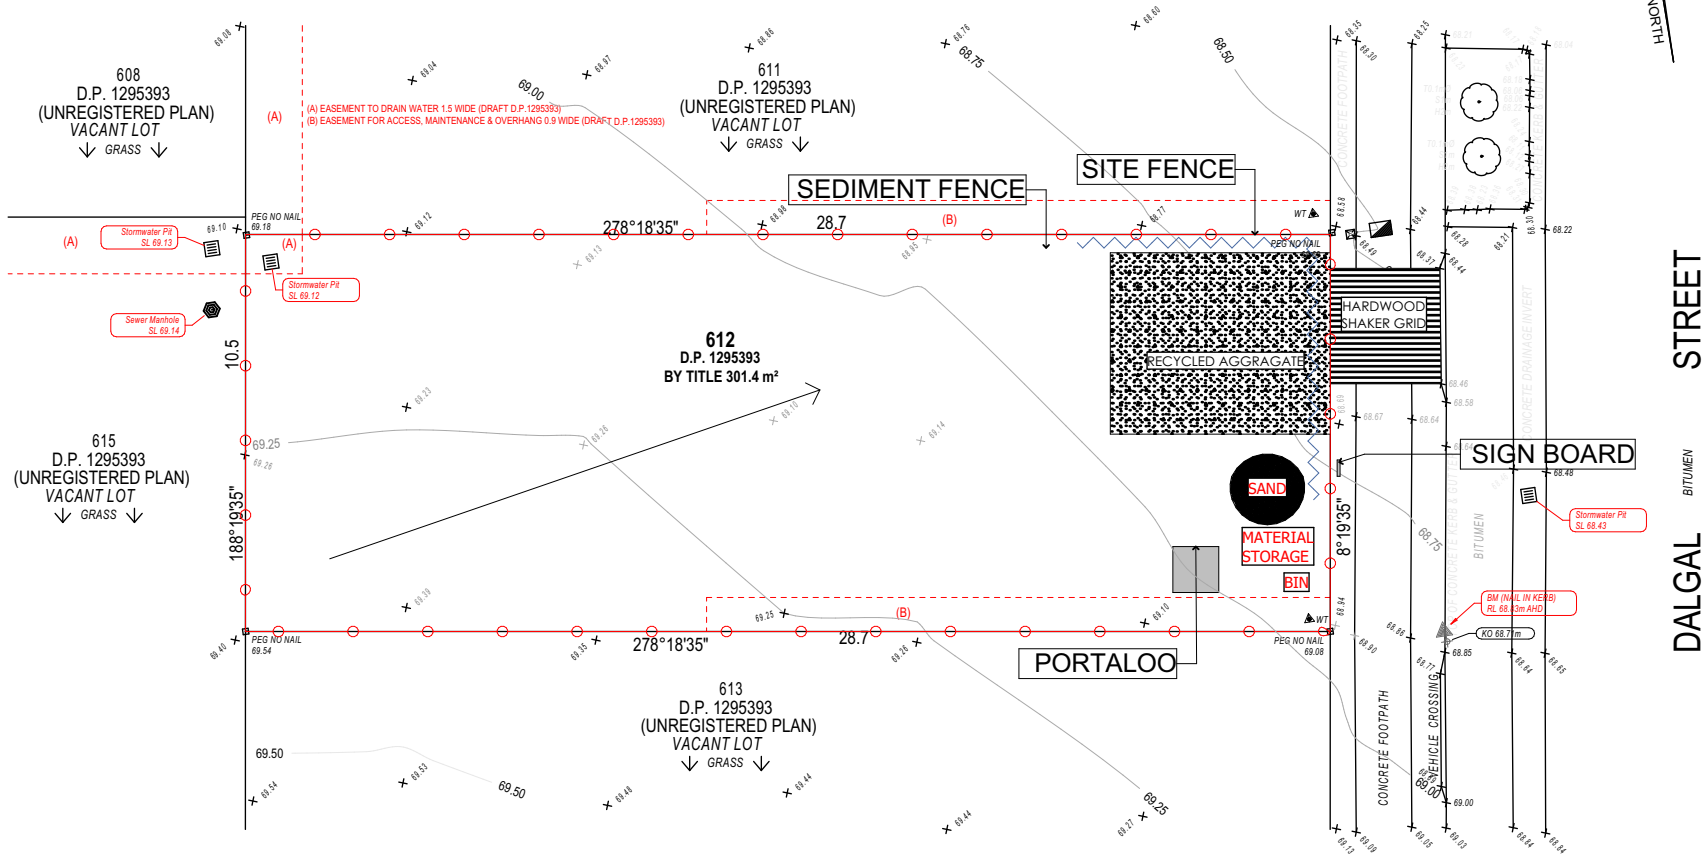

Sediment Control Plan
1:200

NOTE
The Builder shall check all dimensions and levels on site prior to construction. Notify any errors, discrepancies or omissions to the building designer. Refer to written dimensions only. Do not scale drawings. Drawings shall not be used for construction purposes until issued for construction. This drawing reflects a design by Innovative Eco Designs and is to be used only for work when authorised in writing by Innovative Eco Designs.
All boundaries and contours are subject to survey drawing. All levels to Australian Height Data. It is the contractors responsibility to confirm all measurements on site and locations of any services prior to work on site.
All documents here within are subject to Australian Copyright Laws.



37604191460 ABN
(02) 8710 3852
SUITE 7, 4-10 SELEMS PDE
REVESBY, NSW, 2212
design@iedesigns.com.au
www.iedesigns.com.au



B	21-08-2026	Issue for CDC
A	02/08/2026	Issue for CDC



DRAWING : **Sediment Control Plan**
CLIENT : **Sandstone Constructions Pty Ltd**
PROJECT : **PROPOSED DOUBLE STOREY DWELLING**
#7,Dalgat Street,Austral
Lot-612 D.P 1295393

DRAWN BY: NB
SCALE: 1:200
PAGE SIZE A3
DATE : 21-08-2026
APPLICATION : CDC
PAGE NO: 18
PROJECT NO. 2606 920
ISSUE B

