


IMPORTANT NOTE:  
ALL DIMENSIONS AND NOTES ON ALL PLANS MUST BE CHECKED AND VERIFIED BY BUILDER AND  
OR OWNERS PRIOR TO COMMENCEMENT OF ANY BUILDING WORKS TO CLARIFY AND  
CONFIRM WITH PERRAS DESIGN GROUP ANY DISCREPANCIES ON ALL DOCUMENTS AND PLANS  
PROVIDED FOR CONSTRUCTION. ANY WORK INDICATED ON THE PLAN BUT NOT THE  
SPECIFICATION OR VICE VERSA, AND ANY ITEM NOT SHOWN IN EITHER PLAN OR SPECIFICATION  
BUT WHICH IS INDICATED NECESSARY AS PART OF PROPER CONSTRUCTION, OR WHICH IS  
TO BE DONE AS PART OF THE CONTRACT, VARIATIONS TO PLANS SPECIFICATIONS MAY NOT BE  
MADE WITHOUT WRITTEN CONSENT OF THE OWNER. IT IS THE RESPONSIBILITY OF THE BUILDER  
ENGINEER TO VERIFY PLANS AND SPECIFICATIONS AS TO THEIR ACCURACY AND SUSTAINABILITY  
AND ALL SITE WORKS MUST COMPLY WITH CURRENT BCA AND AUSTRALIAN STANDARDS

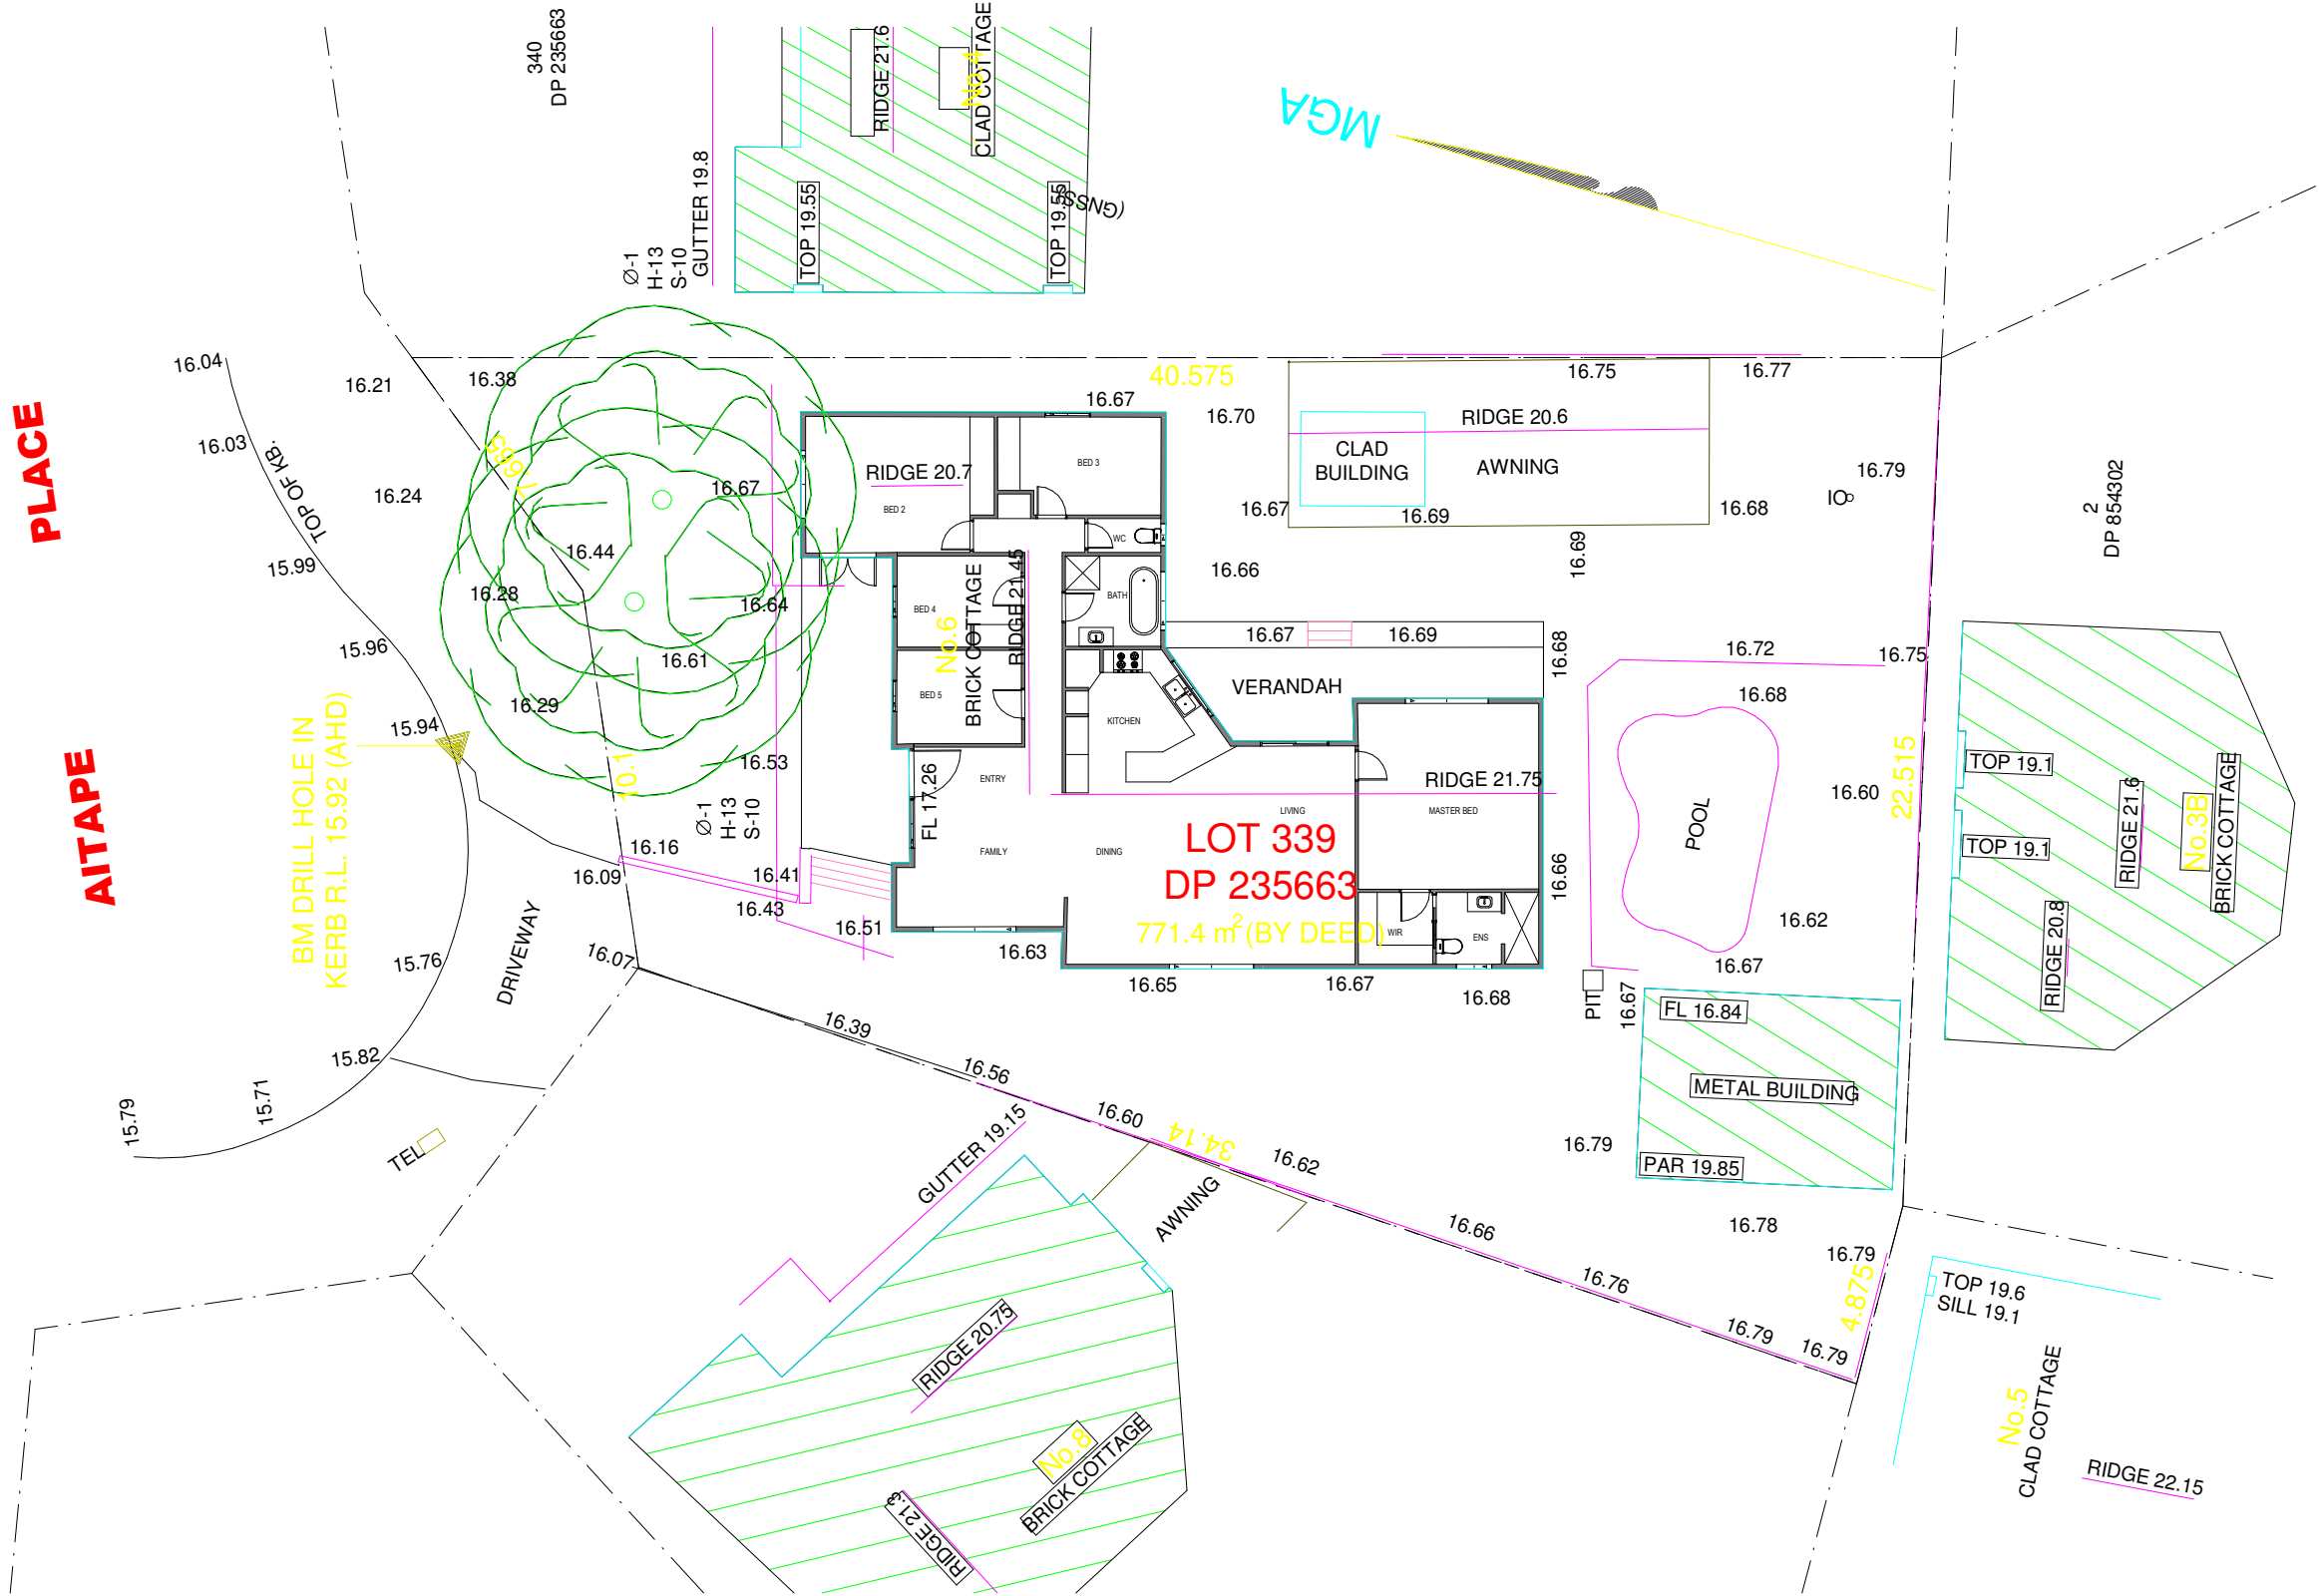

EXISTING FLOOR PLAN  
1:100



PLANS BY...  
**perras design group**

Suite 6, 92 Bathurst Street,  
Liverpool NSW 2170  
Office - (02) 8005 1000  
[www.perrasdesigngroup.com.au](http://www.perrasdesigngroup.com.au)  
PETER PERRAS - DIRECTOR - Mobile 0414 507 259  
Registered Design Practitioner Body Corporate DEP0003999  
Registered Design Practitioner DEP0001985 (All Classes)  
Accredited BDA Aust 6639  
M.BDAA 7488.21



JOB DESCRIPTION  
DEMOLITION AND PROPOSED  
ALTERATION AND ADDITION TO  
EXISTING HOUSE AND PROPOSED  
DETACHED GRANNY FLAT  
AT  
6 AITAPE PLACE, HOLSWORTHY

DRAWING TITLE  
EXISTING PLAN  
CLIENT DETAILS  
FADI YOUSSEF

GENERAL NOTES  
DO NOT SCALE THE DRAWINGS. READ ALL DIMENSIONS SHOWN.  
ALL DIMENSIONS, NOTES ON ALL PLANS AND CONSENT  
DOCUMENTS MUST BE CHECKED AND VERIFIED BY THE  
CONTRACTOR PRIOR TO ANY COMMENCEMENT OF ANY  
BUILDING WORKS ON SITE, TO CLARIFY ANY DISCREPANCIES  
BETWEEN ALL PLAN DRAWINGS AND DOCUMENTATION RELEVANT  
TO THE PROPOSAL / SITE WORKS. GROUND LEVELS MAY VARY  
DUE TO SITE CONDITIONS.  
- COPYRIGHT -  
THESE DRAWINGS REMAIN THE PROPERTY OF PETER PERRAS.  
DIRECTOR OF PERRAS DESIGN GROUP PTY LTD.  
ABN 35 614 757 550 AND CAN NOT BE ALTERED OR REPRODUCED  
WITHOUT WRITTEN CONSENT.

| DRAWN         | M,P      |
|---------------|----------|
| DATE          | JULY.26  |
| CHECKED       | P.PERRAS |
| SCALE         | 1 : 100  |
| JOB NUMBER    | 2684     |
| NUMBER IN SET | 1        |
| ISSUE         | A        |

| REV | AMENDMENTS     | BY  | DATE    |
|-----|----------------|-----|---------|
| A   | CDC SUBMISSION | P.P | JULY.26 |
|     |                |     |         |
|     |                |     |         |
IMPORTANT NOTE:  
ALL DIMENSIONS AND NOTES ON ALL PLANS MUST BE CHECKED AND VERIFIED BY BUILDER AND  
OR OWNER PRIOR TO COMMENCEMENT OF ANY BUILDING WORKS TO CLARIFY AND  
CONFIRM WITH PERRAS DESIGN GROUP ANY DISCREPANCIES ON ALL DOCUMENTS AND PLANS  
PROVIDED FOR CONSTRUCTION. ANY WORK INDICATED ON THE PLAN BUT NOT THE  
SPECIFICATION OR VICE VERSA, AND ANY ITEM NOT SHOWN IN EITHER PLAN OR SPECIFICATION  
BUT WHICH IS INDICATED AS PART OF PROPOSED CONSTRUCTION, OR OTHERWISE  
TO BE DONE AS PART OF THE CONTRACT, UNLESS NOTED TO PLANS SPECIFICATIONS MAY NOT BE  
MADE WITHOUT WRITTEN CONSENT OF THE OWNER. IT IS THE RESPONSIBILITY OF THE BUILDER/  
ENGINEER TO VERIFY PLANS AND SPECIFICATIONS AS TO THEIR ACCURACY AND SUSTAINABILITY  
AND ALL SITE WORKS MUST COMPLY WITH CURRENT BCA AND AUSTRALIAN STANDARDS

| State Environmental Planning Policy<br>(Exempt and<br>Complying Development Codes) 2021 |                      |
|-----------------------------------------------------------------------------------------|----------------------|
| BY TITLE: 771.4m <sup>2</sup>                                                           | LOT 339<br>DP 235663 |
| <b>SITE AREA</b>                                                                        | <b>771.4QM</b>       |
| <b>ALLOWED -</b>                                                                        |                      |
| LANDSCAPE AREA                                                                          | 192.85SQM            |
| LANDSCAPE AREA BEHIND BUILDING LINE                                                     | 96.43SQM             |
| P.O.S AREA                                                                              | 24.05SQM             |
| TOTAL FLOOR AREA                                                                        | 380SQM               |
| SITE COVERAGE                                                                           | 385.7SQM             |
| <b>ACHIEVED -</b>                                                                       |                      |
| LANDSCAPE AREA                                                                          | 220.53SQM            |
| LANDSCAPE AREA BEHIND BUILDING LINE                                                     | 140.67SQM            |
| P.O.S AREA                                                                              | 24SQM                |
| EX/PRO GROUND FLOOR AREA (measured from external walls)                                 | 270.36SQM            |
| PRO. GRANNY FLAT FLOOR AREA (measured from external walls)                              | 60SQM                |
| <b>TOTAL FLOOR AREA</b>                                                                 | <b>330.36SQM</b>     |
| <b>SITE COVERAGE</b>                                                                    | <b>330.36SQM</b>     |

| State Environmental Planning Policy<br>(Exempt and<br>Complying Development Codes) 2008 |                      |
|-----------------------------------------------------------------------------------------|----------------------|
| BY TITLE: 771.4m <sup>2</sup>                                                           | LOT 339<br>DP 235663 |
| <b>SITE AREA</b>                                                                        | <b>771.4QM</b>       |
| <b>ALLOWED -</b>                                                                        |                      |
| LANDSCAPE AREA                                                                          | 231.42SQM            |
| LANDSCAPE AREA BEHIND BUILDING LINE                                                     | 150.94SQM            |
| LANDSCAPE AREA FORWARD BUILDING LINE                                                    | 57.86SQM             |
| P.O.S AREA                                                                              | 24SQM                |
| GROSS FLOOR AREA                                                                        | 335SQM               |
| <b>ACHIEVED -</b>                                                                       |                      |
| LANDSCAPE AREA                                                                          | 239.18SQM            |
| LANDSCAPE AREA BEHIND BUILDING LINE                                                     | 159.32SQM            |
| LANDSCAPE AREA FORWARD BUILDING LINE                                                    | 79.86SQM             |
| P.O.S AREA                                                                              | 24SQM                |
| EX/PROP GROUND FLOOR AREA (measured from internal walls)                                | 236.67SQM            |
| (minus 18sqm garage)                                                                    |                      |
| PROP. GRANNY FLAT AREA (measured from external walls)                                   | 60SQM                |
| <b>GROSS FLOOR AREA(MINUS 18SQM GARAGE)</b>                                             | <b>296.67SQM</b>     |



Suite 6, 92 Bathurst Street,  
Liverpool NSW 2170  
Office - (02) 8005 1000  
[www.perrasdesigngroup.com.au](http://www.perrasdesigngroup.com.au)  
PETER PERRAS - DIRECTOR - Mobile 0414 507 259  
Registered Design Practitioner Body Corporate DEP0003999  
Registered Design Practitioner DEP0001985 (All Classes)  
Accredited BDA Aust 6639  
M.BDAA 7488.21





**JOB DESCRIPTION**  
DEMOLITION AND PROPOSED  
ALTERATION AND ADDITION TO  
EXISTING HOUSE AND PROPOSED  
DETACHED GRANNY FLAT  
  
**AT**  
6 AITAPE PLACE, HOLSWORTHY

**DRAWING TITLE**  
DEMOLITION, SITE & SEDIMENT  
CONTROL PLAN  
  
**CLIENT DETAILS**  
FADI YOUSSEF

**GENERAL NOTES**  
DO NOT SCALE THE DRAWINGS. READ ALL DIMENSIONS SHOWN.  
ALL DIMENSIONS, NOTES ON ALL PLANS AND CONSENT  
DOCUMENTS MUST BE CHECKED AND VERIFIED BY THE  
CONTRACTOR PRIOR TO ANY COMMENCEMENT OF ANY  
BUILDING WORKS ON SITE, TO CLARIFY ANY DISCREPANCIES  
BETWEEN ALL PLAN DRAWINGS AND DOCUMENTATION RELEVANT  
TO THE PROPOSAL / SITE WORKS. GROUND LEVELS MAY VARY  
DUE TO SITE CONDITIONS.  
- COPYRIGHT -  
THESE DRAWINGS REMAIN THE PROPERTY OF PERRAS  
DIRECTOR OF PERRAS DESIGN GROUP PTY LTD.  
ABN 35 614 757 550 AND CAN NOT BE ALTERED OR REPRODUCED  
WITHOUT WRITTEN CONSENT.

|               |          |
|---------------|----------|
| DRAWN         | M.P      |
| DATE          | JULY.26  |
| CHECKED       | P.PERRAS |
| SCALE         | 1 : 100  |
| JOB NUMBER    | 2684     |
| NUMBER IN SET | 2        |
| ISSUE         | A        |

| REV | AMENDMENTS     | BY  | DATE    |
|-----|----------------|-----|---------|
| A   | CDC SUBMISSION | P.P | JULY.26 |
|     |                |     |         |
|     |                |     |         |
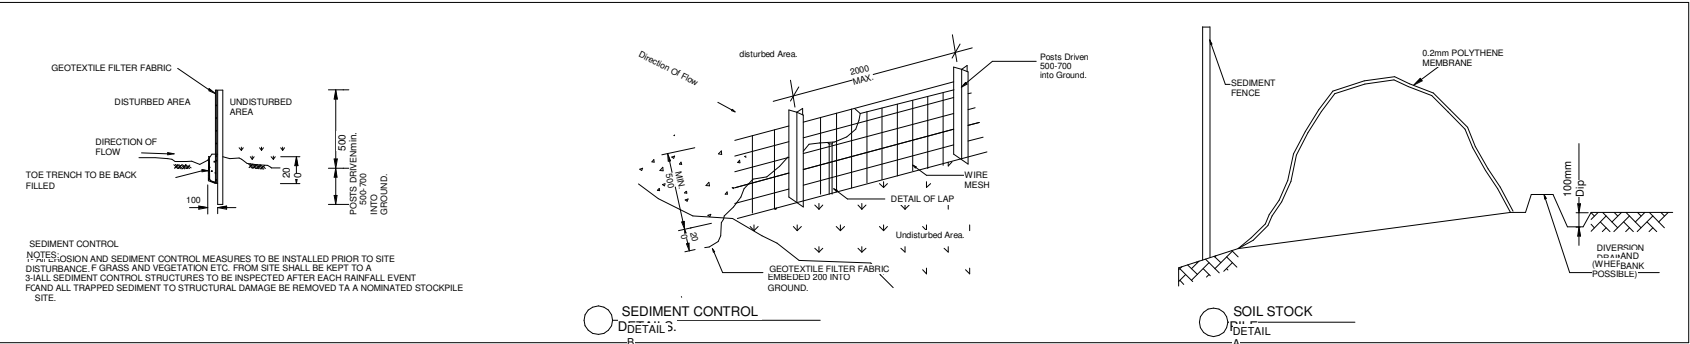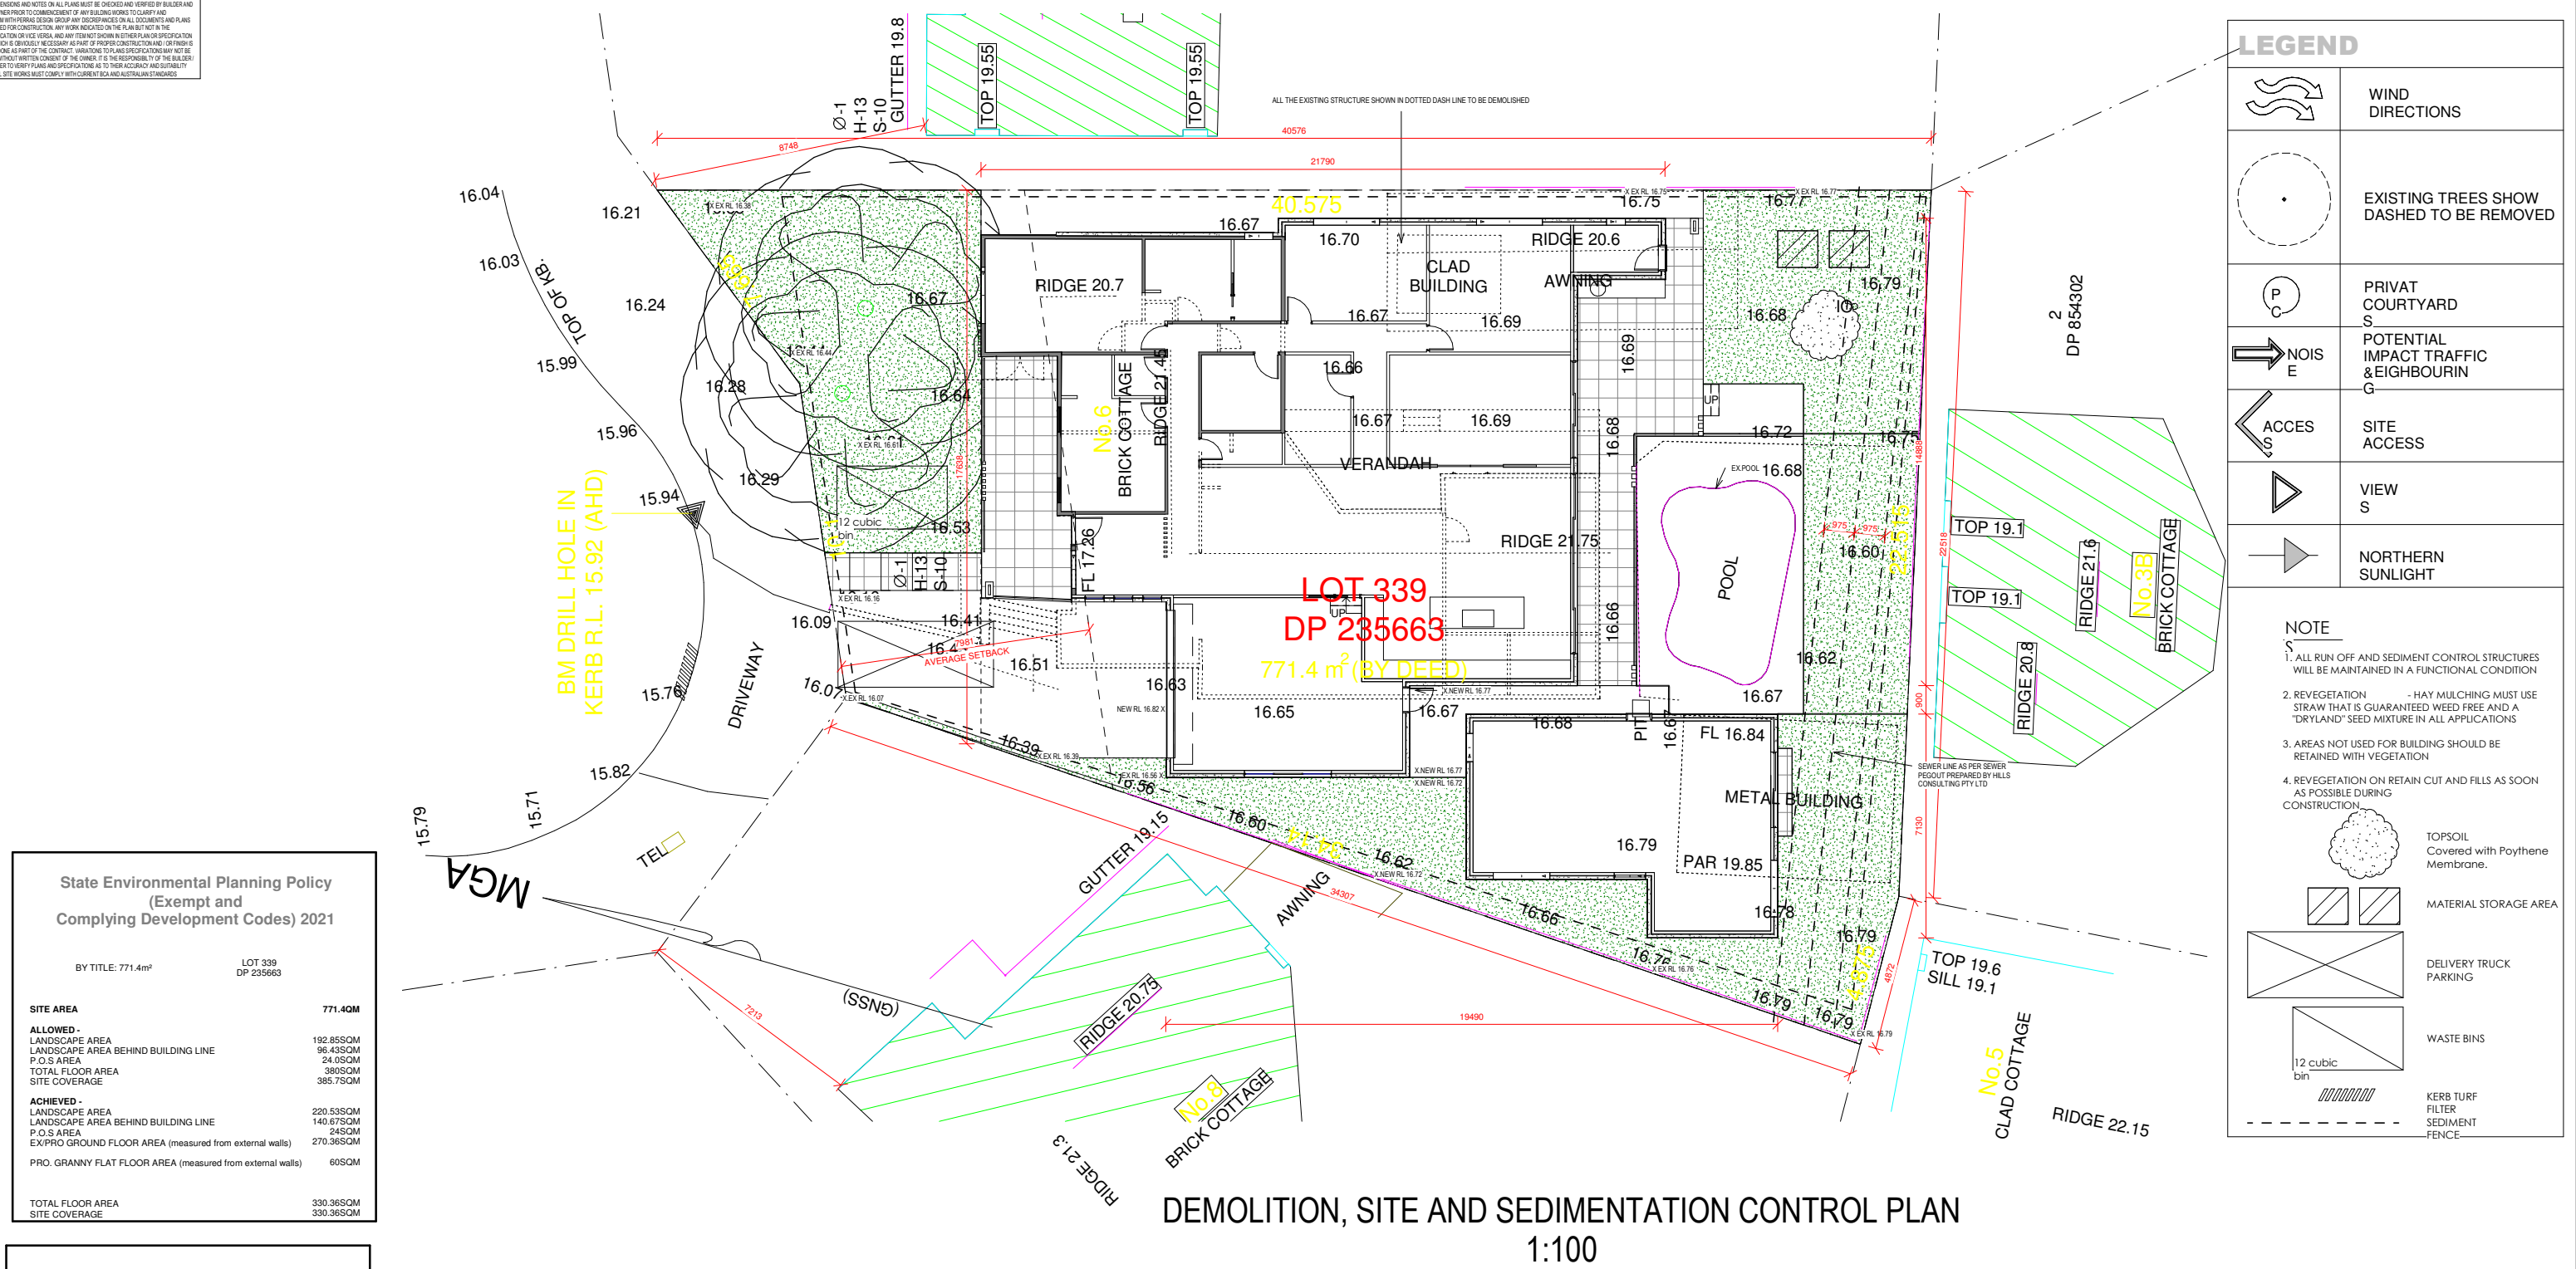

**LEGEND**

- WIND DIRECTIONS
- EXISTING TREES SHOW DASHED TO BE REMOVED
- PRIVAT COURTYARD S
- POTENTIAL IMPACT TRAFFIC & NEIGHBOURIN G
- SITE ACCESS
- VIEW S
- NORTHERN SUNLIGHT


**NOTE**

- ALL RUN OFF AND SEDIMENT CONTROL STRUCTURES WILL BE MAINTAINED IN A FUNCTIONAL CONDITION
- REVEGETATION - HAY MULCHING MUST USE STRAW THAT IS GUARANTEED WEED FREE AND A "DRYLAND" SEED MIXTURE IN ALL APPLICATIONS
- AREAS NOT USED FOR BUILDING SHOULD BE RETAINED WITH VEGETATION
- REVEGETATION ON RETAIN CUT AND FILLS AS SOON AS POSSIBLE DURING CONSTRUCTION

- TOPSOIL Covered with Poythene Membrane.
- MATERIAL STORAGE AREA
- DELIVERY TRUCK PARKING
- WASTE BINS
- KERB TURF FILTER SEDIMENT FENCE

DEMOLITION, SITE AND SEDIMENTATION CONTROL PLAN  
1:100

IMPORTANT NOTE:  
ALL DIMENSIONS AND NOTES ON ALL PLANS MUST BE CHECKED AND VERIFIED BY BUILDER AND/OR OWNER PRIOR TO COMMENCEMENT OF ANY BUILDING WORKS TO CLARIFY AND CONFIRM WITH PERRAS DESIGN GROUP ANY DISCREPANCIES ON ALL DOCUMENTS AND PLANS PROVIDED FOR CONSTRUCTION. ANY WORK INDICATED ON THE PLAN BUT NOT IN THE SPECIFICATION OR VICE VERSA, AND ANY ITEM NOT SHOWN IN EITHER PLAN OR SPECIFICATION BUT WHICH IS INDICATED NECESSARY AS PART OF PROPOSED CONSTRUCTION, IS TO BE DONE AS PART OF THE CONTRACT. VARIATIONS TO PLANS SPECIFICATIONS MAY NOT BE MADE WITHOUT WRITTEN CONSENT OF THE OWNER & IS THE RESPONSIBILITY OF THE BUILDER/ENGINEER TO VERIFY PLANS AND SPECIFICATIONS AS TO THEIR ACCURACY AND SUFFICIENCY AND ALL SITE WORKS MUST COMPLY WITH CURRENT BCA AND AUSTRALIAN STANDARDS.

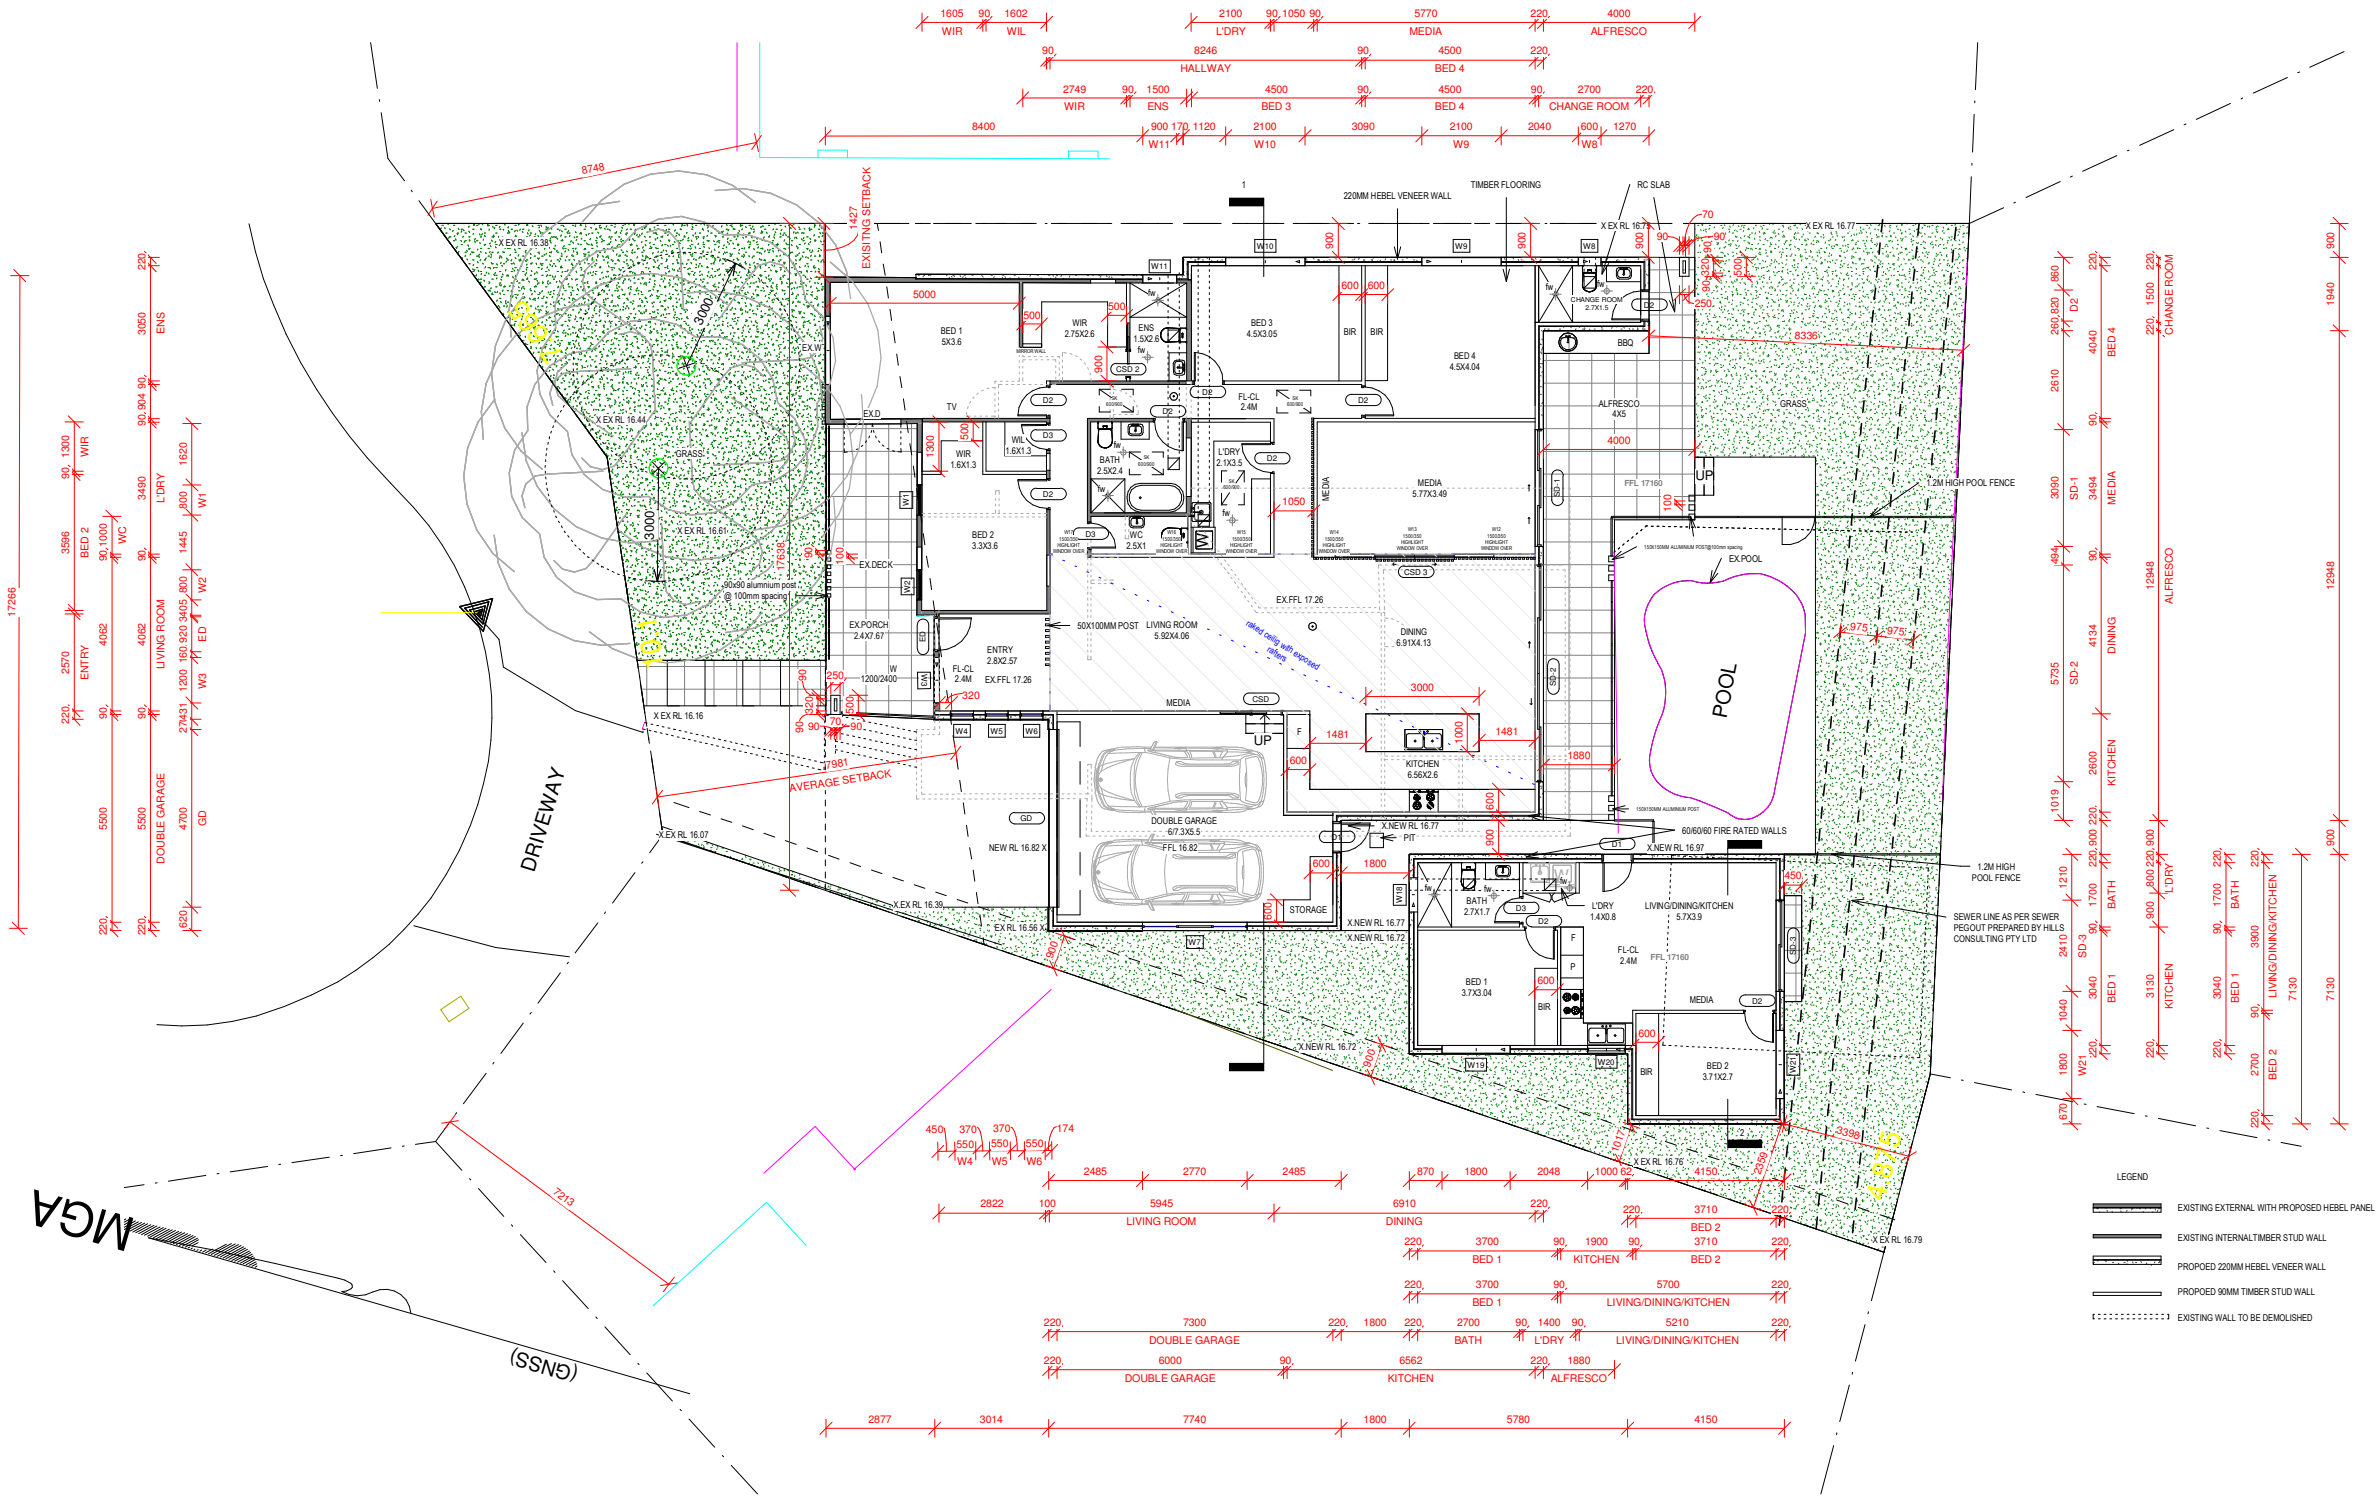

NOTE:

1. All dimensions and notes on all drawings must be checked and verified by client/owner/builder prior to commencement of any building works on site, to clarify any discrepancies between all plans relevant to the proposal/site works.

2. bathrooms and ensuites doors are to be provided with removable hinges.

3. floor waste to all wet floor areas

LEGENDS:

☉ SMOKE ALARM TO COMPLY WITH NCC Codes Vol 2 P2.3.2, CL H3D6

FW FLOOR WASTE

☐ MECHANICAL VENTILATION

GROUND FLOOR PLAN  
1:100

- LEGEND
- EXISTING EXTERNAL WITH PROPOSED HEBEL PANEL
  - EXISTING INTERNAL TIMBER STUD WALL
  - PROPOSED 220MM HEBEL VENEER WALL
  - PROPOSED 90MM TIMBER STUD WALL
  - EXISTING WALL TO BE DEMOLISHED

PLANS BY...

perras design group

Suite 6, 92 Bathurst Street,  
Liverpool NSW 2170  
Office - (02) 8005 1000

www.perrasdesigngroup.com.au

PETER PERRAS - DIRECTOR - Mobile 0414 507 259

Registered Design Practitioner Body Corporate DEP0003999

Registered Design Practitioner DEP0001985 (All Classes)

Accredited BDA Aust 6639

M.BDAA 7488.21



JOB DESCRIPTION

DEMOLITION AND PROPOSED  
ALTERATION AND ADDITION TO  
EXISTING HOUSE AND PROPOSED  
DETACHED GRANNY FLAT

AT

6 AITAPE PLACE, HOLSWORTHY

DRAWING TITLE

GROUND FLOOR PLAN

CLIENT DETAILS

FADI YOUSSEF

GENERAL NOTES

DO NOT SCALE THE DRAWINGS. READ ALL DIMENSIONS SHOWN.  
ALL DIMENSIONS, NOTES ON ALL PLANS AND CONSENT  
DOCUMENTS MUST BE CHECKED AND VERIFIED BY THE  
CONTRACTOR PRIOR TO ANY COMMENCEMENT OF ANY  
BUILDING WORKS ON SITE, TO CLARIFY ANY DISCREPANCIES  
BETWEEN ALL PLAN DRAWINGS AND DOCUMENTATION RELEVANT  
TO THE PROPOSAL / SITE WORKS. GROUND LEVELS MAY VARY  
DUE TO SITE CONDITIONS.

THESE DRAWINGS REMAIN THE PROPERTY OF PETER PERRAS.  
DIRECTOR OF PERRAS DESIGN GROUP PTY LTD.  
ABN 35 614 757 550 AND CAN NOT BE ALTERED OR REPRODUCED  
WITHOUT WRITTEN CONSENT.

DRAWN M.P

DATE JULY.26

CHECKED P.PERRAS

SCALE 1 : 100

JOB NUMBER 2684

NUMBER IN SET 3

ISSUE A

REV

A

CDC SUBMISSION

AMENDMENTS


BY

P.P


DATE

JULY.26

ALL DISCREPANCIES AND NOTES ON ALL PLANS MUST BE CHECKED AND VERIFIED BY BUILDER AND / OR OWNER PRIOR TO COMMENCEMENT OF ANY BUILDING WORKS TO CLARIFY AND CONFORM WITH PERRAS DESIGN GROUP ANY DISCREPANCIES ON ALL DOCUMENTS AND PLANS PROVIDED FOR CONSTRUCTION. ANY WORK INDICATED ON THE PLAN BUT NOT IN THE SPECIFICATION OR VICE VERSA, AND ANY ITEM NOT SHOWN IN EITHER PLAN OR SPECIFICATION BUT WHICH IS OBVIOUSLY NECESSARY AS PART OF PROPER CONSTRUCTION AND / OR FINISH IS TO BE DONE AS PART OF THE CONTRACT. VARIATIONS TO PLANS SPECIFICATIONS MAY NOT BE MADE WITHOUT WRITTEN CONSENT OF THE OWNER. IT IS THE RESPONSIBILITY OF THE BUILDER / END USER TO VERIFY PLANS AND SPECIFICATIONS AS TO THEIR ACCURACY AND SUITABILITY AND ALL SITE WORKS MUST COMPLY WITH CURRENT BCA AND AUSTRALIAN STANDARDS

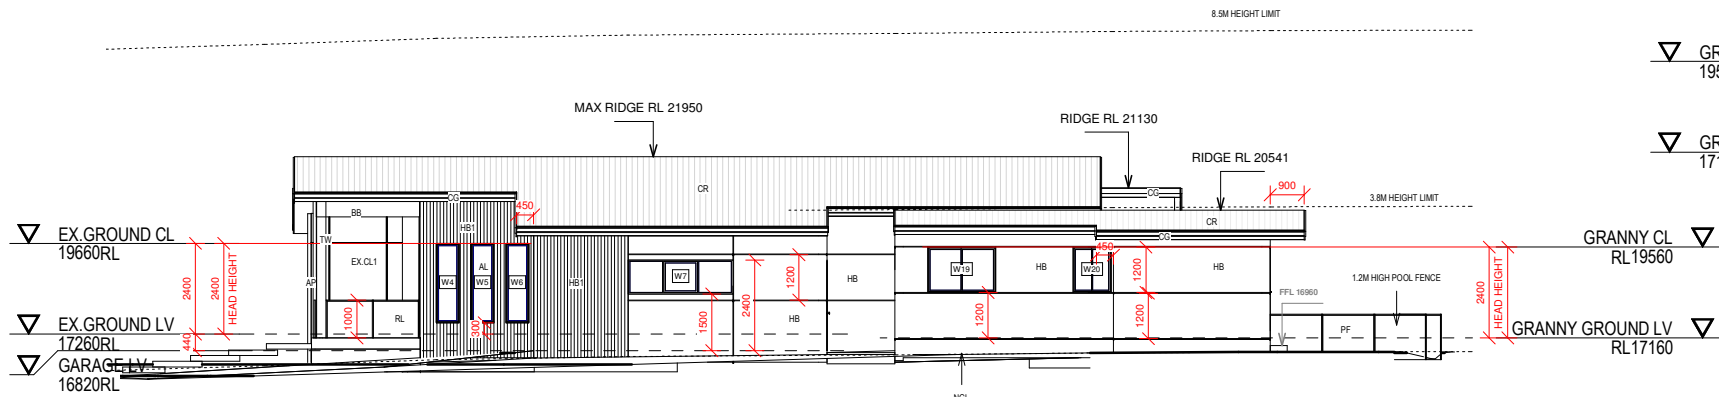

WEST ELEVATION  
1:100

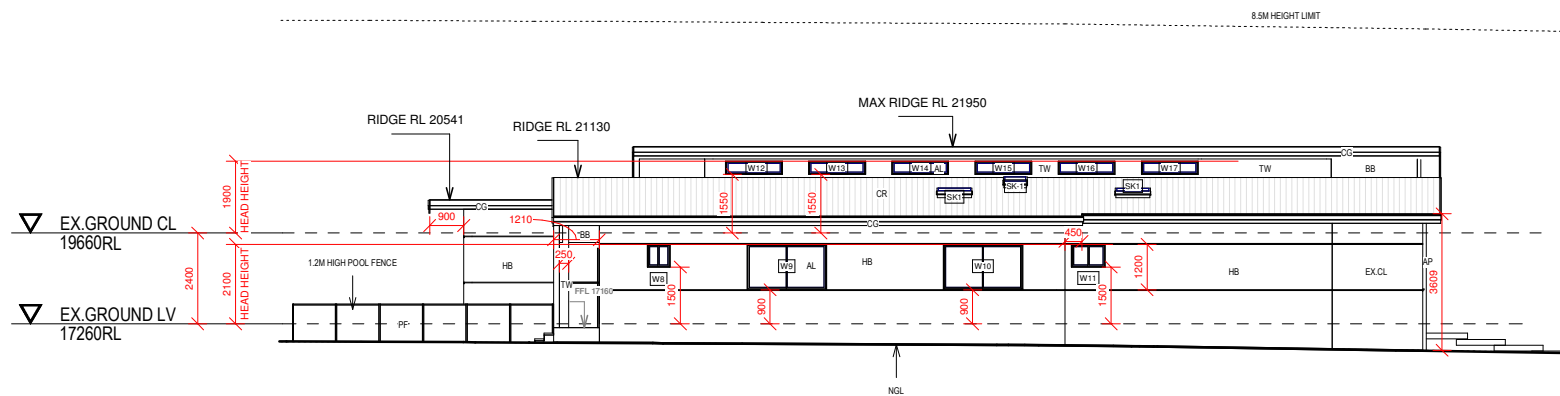


EAST ELEVATION  
1:100


| DOOR SCHEDULE       |                  |       |        |             |       |                                    |
|---------------------|------------------|-------|--------|-------------|-------|------------------------------------|
| DOOR NO.            | FLOOR LEVEL      | WIDTH | HEIGHT | HEAD HEIGHT | COUNT | DESCRIPTION                        |
| GARAGE LV           |                  |       |        |             |       |                                    |
| D1                  | GARAGE LV        | 820   | 2400   | 2400        | 1     | TIMBER FRAME SWING DOOR            |
| GD                  | GARAGE LV        | 4700  | 2400   | 2400        | 1     | GARAGE PANEL LIFT DOOR             |
| GARAGE LV: 2        |                  |       |        |             |       |                                    |
| GRANNY GROUND LV    |                  |       |        |             |       |                                    |
| D1                  | GRANNY GROUND LV | 820   | 2400   | 2400        | 1     | TIMBER FRAME SWING DOOR            |
| D2                  | GRANNY GROUND LV | 820   | 2100   | 2100        | 2     | TIMBER FRAME SWING DOOR            |
| D3                  | GRANNY GROUND LV | 720   | 2100   | 2100        | 1     | TIMBER FRAME SWING DOOR            |
| SD-3                | GRANNY GROUND LV | 2410  | 2400   | 2400        | 1     | ALUMINIUM FRAME GLASS SLIDING DOOR |
| GRANNY GROUND LV: 5 |                  |       |        |             |       |                                    |
| EX.GROUND LV        |                  |       |        |             |       |                                    |
| CSD                 | EX.GROUND LV     | 820   | 2100   | 2100        | 1     | TIMBER FRAME CAVITY SLIDING DOOR   |
| CSD 2               | EX.GROUND LV     | 720   | 2100   | 2100        | 2     | TIMBER FRAME CAVITY SLIDING DOOR   |
| CSD 3               | EX.GROUND LV     | 2100  | 2100   | 2100        | 1     | TIMBER FRAME CAVITY SLIDING DOOR   |
| D1                  | EX.GROUND LV     | 820   | 2400   | 2400        | 7     | TIMBER FRAME SWING DOOR            |
| D2                  | EX.GROUND LV     | 820   | 2100   | 2100        | 7     | TIMBER FRAME SWING DOOR            |
| D3                  | EX.GROUND LV     | 720   | 2100   | 2100        | 3     | TIMBER FRAME SWING DOOR            |
| ED                  | EX.GROUND LV     | 920   | 2400   | 2400        | 1     | TIMBER FRAME ENTRY DOOR            |
| SD-1                | EX.GROUND LV     | 3090  | 2400   | 2400        | 1     | ALUMINIUM FRAME GLASS SLIDING DOOR |
| SD-2                | EX.GROUND LV     | 5735  | 2400   | 2400        | 1     | ALUMINIUM FRAME GLASS SLIDING DOOR |
| EX.GROUND LV: 24    |                  |       |        |             |       |                                    |
| Grand total: 31     |                  |       |        |             |       |                                    |

| WINDOW SCHEDULE    |       |        |             |       |                                       |
|--------------------|-------|--------|-------------|-------|---------------------------------------|
| WINDOW NO          | WIDTH | HEIGHT | HEAD HEIGHT | COUNT | DESCRIPTION                           |
| GARAGE LV          |       |        |             |       |                                       |
| W7                 | 2770  | 900    | 2400        | 1     | ALUMINIUM FRAME GLASS SLIDING WINDOW  |
| GARAGE LV: 1       |       |        |             |       |                                       |
| GRANNY GROUP LV    |       |        |             |       |                                       |
| W18                | 900   | 600    | 2400        | 1     | ALUMINIUM FRAME GLASS SLIDING WINDOW  |
| W19                | 1800  | 1200   | 2400        | 1     | ALUMINIUM FRAME GLASS SLIDING WINDOW  |
| W20                | 1000  | 1200   | 2400        | 1     | ALUMINIUM FRAME GLASS SLIDING WINDOW  |
| W21                | 1800  | 1200   | 2400        | 1     | ALUMINIUM FRAME GLASS SLIDING WINDOW  |
| GRANNY GROUP LV: 4 |       |        |             |       |                                       |
| EX.GROUND LV       |       |        |             |       |                                       |
| W1                 | 800   | 1800   | 2400        | 1     | ALUMINIUM FRAME GLASS TOP HUNG WINDOW |
| W2                 | 800   | 1800   | 2400        | 1     | ALUMINIUM FRAME GLASS TOP HUNG WINDOW |
| W3                 | 1200  | 2400   | 2400        | 1     | ALUMINIUM FRAME GLASS SLIDING WINDOW  |
| W4                 | 600   | 2100   | 2400        | 1     | ALUMINIUM FRAME GLASS FIXED WINDOW    |
| W5                 | 600   | 2100   | 2400        | 1     | ALUMINIUM FRAME GLASS FIXED WINDOW    |
| W6                 | 600   | 2100   | 2400        | 1     | ALUMINIUM FRAME GLASS FIXED WINDOW    |
| W8                 | 600   | 600    | 2100        | 1     | ALUMINIUM FRAME GLASS SLIDING WINDOW  |
| W9                 | 2100  | 1200   | 2100        | 1     | ALUMINIUM FRAME GLASS SLIDING WINDOW  |
| W10                | 2100  | 1200   | 2100        | 1     | ALUMINIUM FRAME GLASS SLIDING WINDOW  |
| W11                | 900   | 600    | 2100        | 1     | ALUMINIUM FRAME GLASS SLIDING WINDOW  |
| EX.GROUND LV: 10   |       |        |             |       |                                       |
| EX.GROUND CL       |       |        |             |       |                                       |
| W12                | 1500  | 350    | 1900        | 1     | ALUMINIUM FRAME GLASS FIXED WINDOW    |
| W13                | 1500  | 350    | 1900        | 1     | ALUMINIUM FRAME GLASS FIXED WINDOW    |
| W14                | 1500  | 350    | 1900        | 1     | ALUMINIUM FRAME GLASS FIXED WINDOW    |
| W15                | 1500  | 350    | 1900        | 1     | ALUMINIUM FRAME GLASS FIXED WINDOW    |
| W16                | 1500  | 350    | 1900        | 1     | ALUMINIUM FRAME GLASS FIXED WINDOW    |
| W17                | 1500  | 350    | 1900        | 1     | ALUMINIUM FRAME GLASS FIXED WINDOW    |
| EX.GROUND CL: 6    |       |        |             |       |                                       |
| Grand total: 21    |       |        |             |       |                                       |

| GROUND LEVEL - WINDOWS SCHEDULE   |              |               |             |                 |          |
|---|--------------|---------------|-------------|-----------------|----------|
| WINDOW NO.   | WINDOW WIDTH | WINDOW HEIGHT | HEAD HEIGHT | DESCRIPTION     | QUANTITY |
| SK-1   | 600          | 900           | -           | SKYLIGHT WINDOW | 3        |
| <p align="center"><b>IMPORTANT NOTE:</b></p> <p align="center">All windows to comply with Clause D2.24 of NCC Volume One, and clauses 3.2.6.2 and 3.9.2.7 of NCC Volume Two<br/> PLEASE REFER TO ELEVATION FOR WINDOWS STYLE &amp; GLASS TYPE</p> |              |               |             |                 |          |

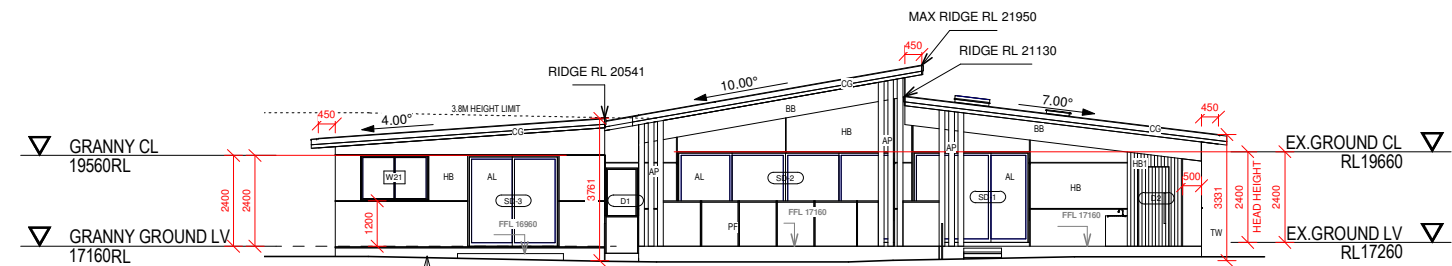

SOUTH ELEVATION  
1:100

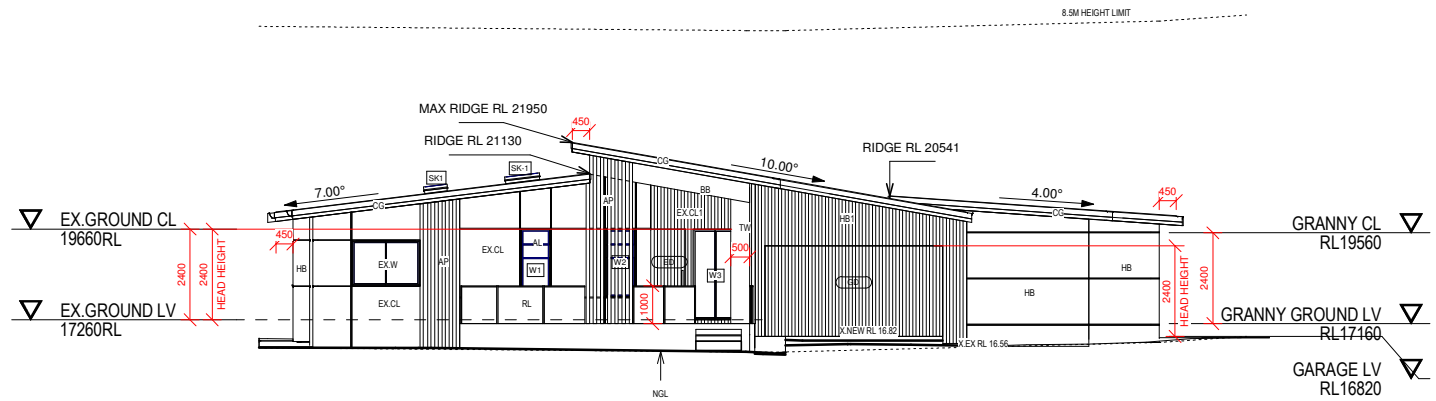

NORTH ELEVATION  
1:100


**LEGEND:**

CR - COLORBOND METAL ROOF - SHALE GREY OR SIMILAR  
CG - COLORBOND FASCIA GUTTER & DOWN PIPES - SHALE GREY OR SIMILAR  
EX.W - EXISTING WINDOW  
EX.D - EXISTING DOOR  
EX.CL - EXISTING WALL WITH PROPOSED TEXTURED CONCRETE RENDER  
EX.CL.1 - EXISTING WALL WITH PROPOSED VERTICAL TIMBER CLADDING  
HB - 220MM HEBEL VENEER WALL WITH TEXTURED CONCRETE RENDER  
HB.220 - 220MM HEBEL VENEER WALL WITH VERTICAL TIMBER CLADDING  
TW - TIMBER STUD WALL WITH RENDER AND PAINT FINISH - DULUX WHITE OR SIMILAR  
BL - BLUE BOARD WITH RENDER AND PAINT FINISH - DULUX WHITE OR SIMILAR  
ED - ENTRY DOOR WITH VERTICAL TIMBER CLADDING  
GD - GARAGE PANEL ENTRY DOOR WITH VERTICAL TIMBER CLADDING  
AP - ALUMINIUM POST  
AL - ALUMINIUM FRAMED WINDOWS, DOORS AND SLIDING DOORS  
NLG - ALUMINIUM GROUND LINE  
PGL - PROPOSED GROUND LINE  
PL - SELECTED POWDER COATED RAILING  
P.1.2M HIGH POOL FENCE


**NOTE - SEE COLOUR SCHEDULE FOR FINISHES**

| <br><b>ACCREDITED</b><br>BUILDING DESIGNER | JOB DESCRIPTION   | DRAWING TITLE                  | GENERAL NOTES   | DRAWN    | M,P     | REV | AMENDMENTS |  | BY | DATE |
|---|---|--------------------------------|---|----------|---------|-----|------------|--|----|------|
|   | DEMOLITION AND PROPOSED ALTERATION AND ADDITION TO EXISTING HOUSE AND PROPOSED DETACHED GRANNY FLAT<br><br>AT<br><br>6 AITAPE PLACE, HOLSWORTHY | ELEVATIONS AND WINDOW SCHEDULE | DO NOT SCALE THE DRAWINGS. READ ALL DIMENSIONS SHOWN. ALL DIMENSIONS, NOTES ON ALL PLANS AND CONSENT DOCUMENTS MUST BE CHECKED AND VERIFIED BY THE CONTRACTOR PRIOR TO ANY COMMENCEMENT OF ANY BUILDING WORKS ON SITE. TO CLARIFY ANY DISCREPANCIES BETWEEN ALL PLAN DRAWINGS AND DOCUMENTATION RELEVANT TO THE PROPOSAL / SITE WORKS. GROUND LEVELS MAY VARY DUE TO SITE CONDITIONS.<br>COPYRIGHT -<br>THESE DRAWINGS REMAIN THE PROPERTY OF PETER PERRAS, DIRECTOR OF PERRAS DESIGN GROUP PTY LTD.<br>ABN 35 614 757 550 AND CAN NOT BE ALTERED OR REPRODUCED WITHOUT WRITTEN CONSENT. | DATE     | JULY.26 |     |            |  |    |      |
|   |   | CHECKED                        |   | P.PERRAS |         |     |            |  |    |      |
|   |   | SCALE                          |   | 1 : 100  |         |     |            |  |    |      |
|   |   | JOB NUMBER                     |   | 2684     |         |     |            |  |    |      |
|   |   | NUMBER IN SET                  |   | 4        |         |     |            |  |    |      |
|   |   | ISSUE                          |   | A        |         |     |            |  |    |      |


IMPORTANT NOTE:  
ALL DIMENSIONS AND NOTES ON ALL PLANS MUST BE CHECKED AND VERIFIED BY BUILDER AND  
OR OWNER PRIOR TO COMMENCEMENT OF ANY BUILDING WORKS TO CLARIFY AND  
CONFIRM WITH PERRAS DESIGN GROUP ANY DISCREPANCIES ON ALL DOCUMENTS AND PLANS  
PROVIDED FOR CONSTRUCTION. ANY WORK INDICATED ON THE PLAN BUT NOT IN THE  
SPECIFICATION OR VICE VERSA, AND ANY ITEM NOT SHOWN IN EITHER PLAN OR SPECIFICATION  
BUT WHICH IS DEEMED NECESSARY AS PART OF PROPOSED CONSTRUCTION, OR OTHERWISE  
TO BE DONE AS PART OF THE CONTRACT, VARIATIONS TO PLANS/SPECIFICATIONS MAY NOT BE  
MADE WITHOUT WRITTEN CONSENT OF THE OWNER & IS THE RESPONSIBILITY OF THE BUILDER.  
ENGINEER TO VERIFY PLANS AND SPECIFICATIONS AS TO THEIR ACCURACY AND SUITABILITY  
AND ALL SITE WORKS MUST COMPLY WITH CURRENT BCA AND AUSTRALIAN STANDARDS

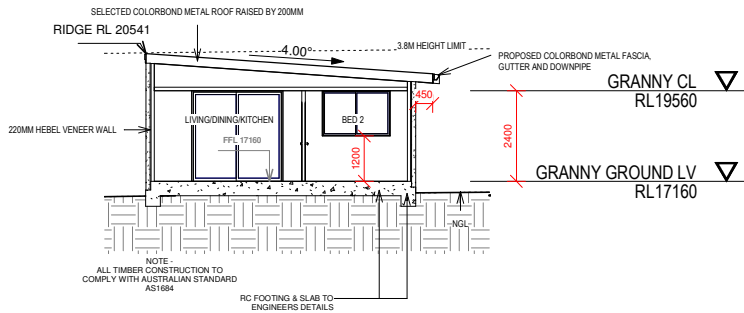

SECTION 2  
1:100

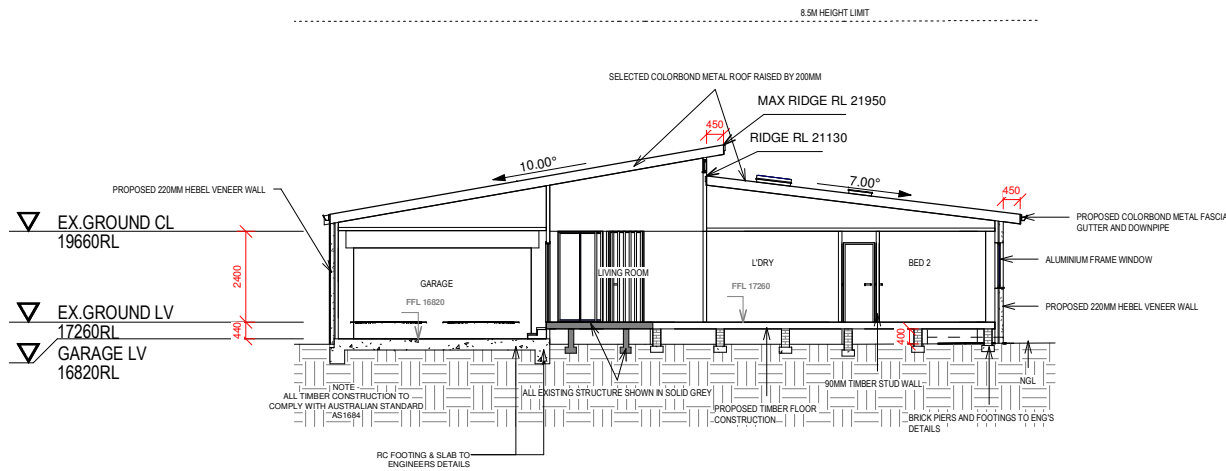

SECTION 1  
1:100

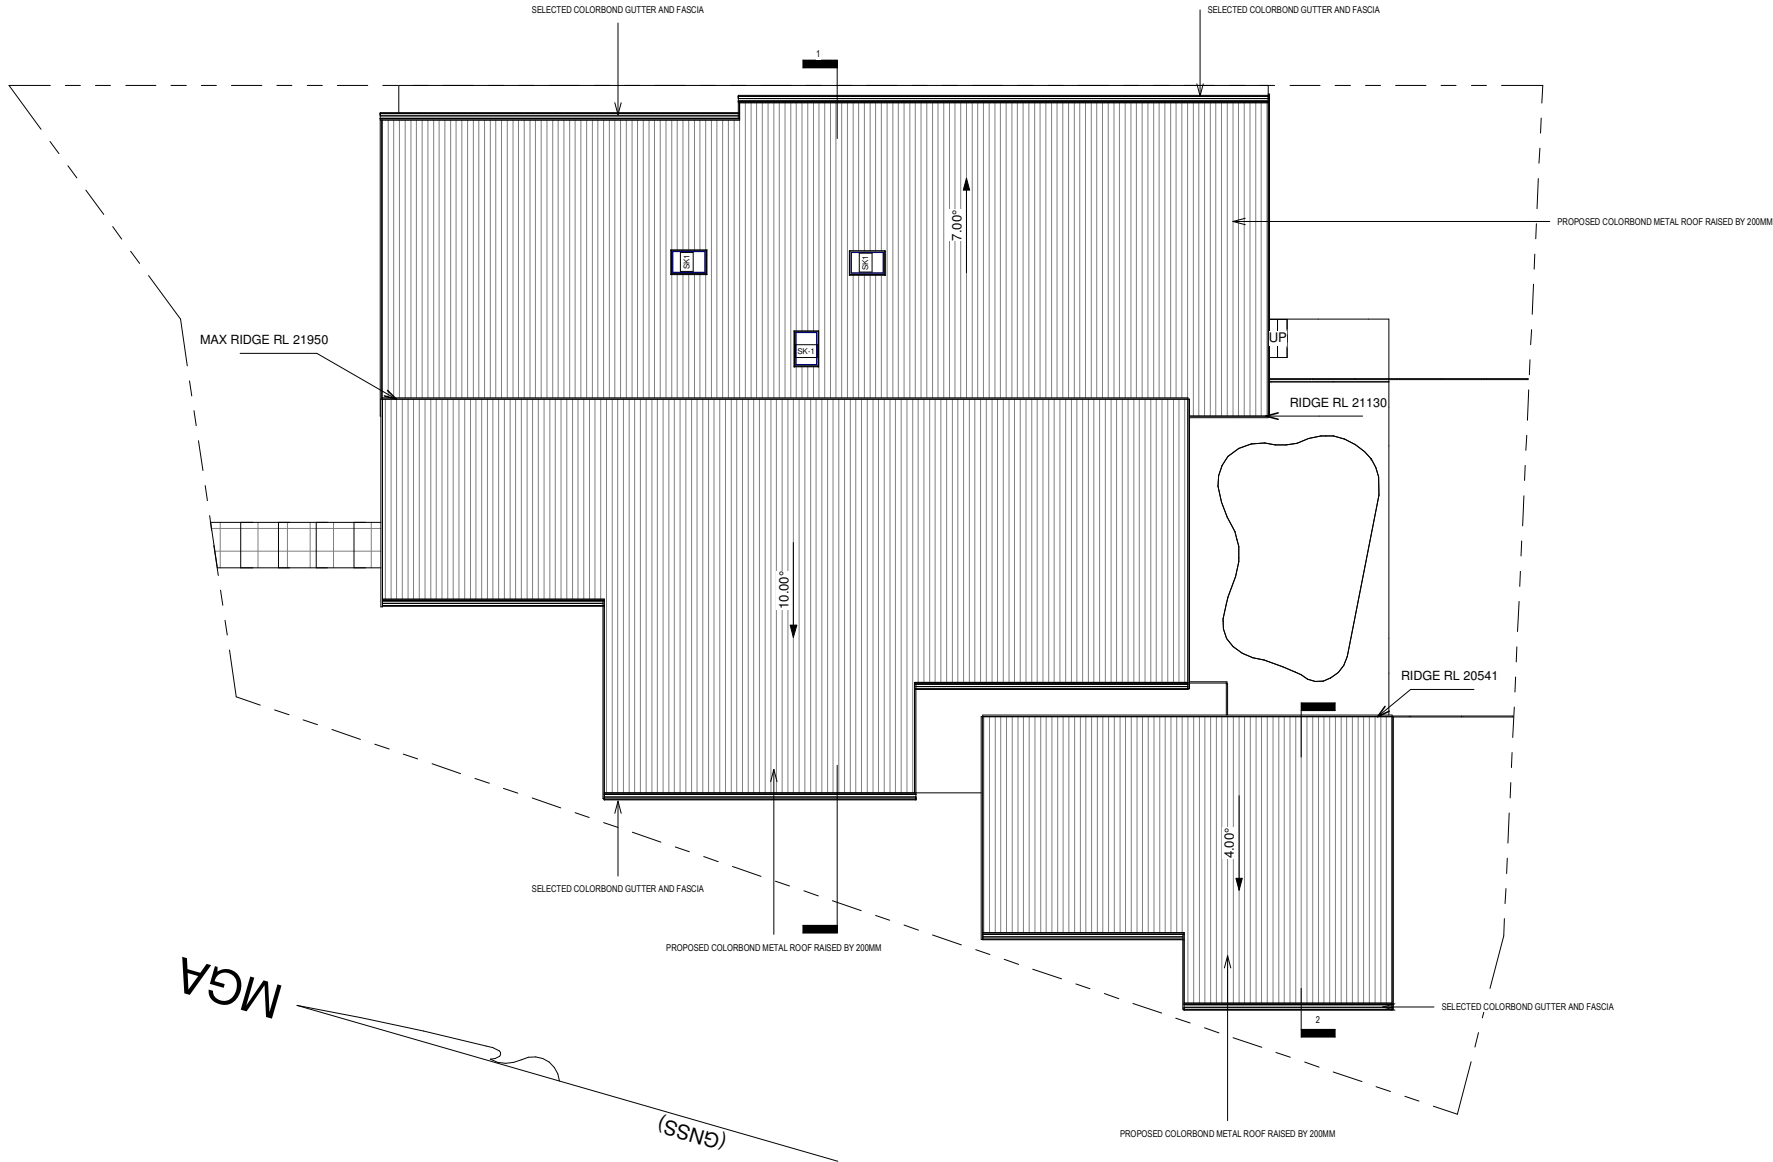

ROOF PLAN  
1:100



PLANS BY...  
**perras design group**

Suite 6, 92 Bathurst Street,  
Liverpool NSW 2170  
Office - (02) 8005 1000

[www.perrasdesigngroup.com.au](http://www.perrasdesigngroup.com.au)  
PETER PERRAS - DIRECTOR - Mobile 0414 507 259  
Registered Design Practitioner Body Corporate DEP0003999  
Registered Design Practitioner DEP0001985 (All Classes)  
Accredited BDA Aust 6639  
M.BDAA 7488.21



ACCREDITED  
BUILDING DESIGNER

| JOB DESCRIPTION                                                                                     | DRAWING TITLE                  |
|---|--------------------------------|
| DEMOLITION AND PROPOSED ALTERATION AND ADDITION TO EXISTING HOUSE AND PROPOSED DETACHED GRANNY FLAT | ROOF PLAN AND SECTION          |
| AT<br>6 AITAPE PLACE, HOLSWORTHY                                                                    | CLIENT DETAILS<br>FADI YOUSSEF |

| GENERAL NOTES   |
|---|
| DO NOT SCALE THE DRAWINGS. READ ALL DIMENSIONS SHOWN. ALL DIMENSIONS, NOTES ON ALL PLANS AND CONSENT DOCUMENTS MUST BE CHECKED AND VERIFIED BY THE CONTRACTOR PRIOR TO ANY COMMENCEMENT OF ANY BUILDING WORKS ON SITE, TO CLARIFY ANY DISCREPANCIES BETWEEN ALL PLAN DRAWINGS AND DOCUMENTATION RELEVANT TO THE PROPOSAL / SITE WORKS. GROUND LEVELS MAY VARY DUE TO SITE CONDITIONS. |
| - COPYRIGHT -<br>THESE DRAWINGS REMAIN THE PROPERTY OF PETER PERRAS, DIRECTOR OF PERRAS DESIGN GROUP PTY LTD. ABN 35 614 757 550 AND CAN NOT BE ALTERED OR REPRODUCED WITHOUT WRITTEN CONSENT.   |

| DRAWN         | M,P      |
|---------------|----------|
| DATE          | JULY.26  |
| CHECKED       | P.PERRAS |
| SCALE         | 1 : 100  |
| JOB NUMBER    | 2684     |
| NUMBER IN SET | 5        |
| ISSUE         | A        |

| REV | AMENDMENTS     | BY  | DATE    |
|-----|----------------|-----|---------|
| A   | CDC SUBMISSION | P.P | JULY.26 |
|     |                |     |         |
|     |                |     |         |
IMPORTANT NOTE:  
ALL DIMENSIONS AND NOTES ON ALL PLANS MUST BE CHECKED AND VERIFIED BY BUILDER AND  
OR OWNERS PRIOR TO COMMENCEMENT OF ANY BUILDING WORKS TO CLARIFY AND  
CONFIRM WITH PERRAS DESIGN GROUP ANY DISCREPANCIES ON ALL DOCUMENTS AND PLANS  
PROVIDED FOR CONSTRUCTION. ANY WORK INDICATED ON THE PLAN BUT NOT IN THE  
SPECIFICATION OR VICE VERSA AND ANY ITEM NOT SHOWN IN EITHER PLAN OR SPECIFICATION  
BUT WHICH IS INDICATED NECESSARY AS PART OF PROPOSED CONSTRUCTION (E.G. FENCES) IS  
TO BE DONE AS PART OF THE CONTRACT. VARIATIONS TO PLANS/SPECIFICATIONS MAY NOT BE  
MADE WITHOUT WRITTEN CONSENT OF THE OWNER. IT IS THE RESPONSIBILITY OF THE BUILDER/  
ENGINEER TO VERIFY PLANS AND SPECIFICATIONS AS TO THEIR ACCURACY AND SUSTAINABILITY  
AND ALL SITE WORKS MUST COMPLY WITH CURRENT BCA AND AUSTRALIAN STANDARDS



LEGEND:

- CR - COLORBOND METAL ROOF - SHALE GREY OR SIMILAR  
CG - COLORBOND FASCIA GUTTER & DOWN PIPES - SHALE GREY OR SIMILAR  
EX.W - EXISTING WINDOW  
EX.D - EXISTING DOOR  
EX.CL - EXISTING WALL WITH PROPOSED TEXTURED CONCRETE RENDER  
EX.CL.1 - EXISTING WALL WITH PROPOSED VERTICAL TIMBER CLADDING  
HB- 220MM HEBEL VENEER WALL WITH TEXTURED CONCRETE RENDER  
HB1- 220MM HEBEL VENEER WALL WITH VERTICAL TIMBER CLADDING  
TW- TIMBER STUD WALL WITH RENDER AND PAINT FINISH - DULUX WHITE OR SIMILAR  
BB - BLUE BOARD WITH RENDER AND PAINT FINISH - DULUX WHITE OR SIMILAR  
ED- ENTRY DOOR WITH VERTICAL TIMBER CLADDING  
GD- GARAGE PANEL ENTRY DOOR WITH VERTICAL TIMBER CLADDING  
AP- ALUMINIUM POST  
AL - ALUMINIUM FRAMED WINDOWS, DOORS AND SLIDING DOORS  
NGL - NATURAL GROUND LINE  
PGL - PROPOSED GROUND LINE  
RL - SELECTED POWDER COATED RAILING  
PF - 1.2M HIGH POOL FENCE



PLANS BY...



perras design group

Suite 6, 92 Bathurst Street,  
Liverpool NSW 2170  
Office - (02) 8005 1000

[www.perrasdesigngroup.com.au](http://www.perrasdesigngroup.com.au)

PETER PERRAS - DIRECTOR - Mobile 0414 507 259

Registered Design Practitioner Body Corporate DEP0003999  
Registered Design Practitioner DEP0001985 (All Classes)  
Accredited BDA Aust 6639  
M.BDAA 7488.21



JOB DESCRIPTION

DEMOLITION AND PROPOSED  
ALTERATION AND ADDITION TO  
EXISTING HOUSE AND PROPOSED  
DETACHED GRANNY FLAT

AT  
6 AITAPE PLACE, HOLSWORTHY

DRAWING TITLE

COLOR SCHEDULE/3D RENDERS

CLIENT DETAILS

FADI YOUSSEF

GENERAL NOTES

DO NOT SCALE THE DRAWINGS. READ ALL DIMENSIONS SHOWN.  
ALL DIMENSIONS, NOTES ON ALL PLANS AND CONSENT  
DOCUMENTS MUST BE CHECKED AND VERIFIED BY THE  
CONTRACTOR PRIOR TO ANY COMMENCEMENT OF ANY  
BUILDING WORKS ON SITE, TO CLARIFY ANY DISCREPANCIES  
BETWEEN ALL PLAN DRAWINGS AND DOCUMENTATION RELEVANT  
TO THE PROPOSAL / SITE WORKS. GROUND LEVELS MAY VARY  
DUE TO SITE CONDITIONS.

- COPYRIGHT -  
THESE DRAWINGS REMAIN THE PROPERTY OF PETER PERRAS,  
DIRECTOR OF PERRAS DESIGN GROUP PTY LTD.  
ABN 35 614 757 550 AND CAN NOT BE ALTERED OR REPRODUCED  
WITHOUT WRITTEN CONSENT.

| DRAWN         | M,P      |
|---------------|----------|
| DATE          | JULY.26  |
| CHECKED       | P.PERRAS |
| SCALE         | N/A      |
| JOB NUMBER    | 2684     |
| NUMBER IN SET | 6        |
| ISSUE         | A        |

| REV | AMENDMENTS     | BY  | DATE    |
|-----|----------------|-----|---------|
| A   | CDC SUBMISSION | P,P | JULY.26 |
|     |                |     |         |
|     |                |     |         |
PLANS BY...

**perras** design group

Suite 6, 92 Bathurst Street,  
Liverpool NSW 2170  
Office - (02) 8005 1000  
[www.perrasdesigngroup.com.au](http://www.perrasdesigngroup.com.au)  
PETER PERRAS - DIRECTOR - Mobile 0414 507 259  
Registered Design Practitioner Body Corporate DEP0003999  
Registered Design Practitioner DEP0001985 (All Classes)  
Accredited BDA Aust 6639  
M.BDAA 7488.21

**ACCREDITED**  
BUILDING DESIGNER

|                  |
|------------------|
| DRAWING TITLE    |
| BASIX COMMENTS-1 |
| CLIENT DETAILS   |
| FADI YOUSSEF     |

## GENERAL NOTES

1. ALL THE DRAWINGS, READ ALL DIMENSIONS SHOWN. DIMENSIONS, NOTES ON ALL PLANS AND CONSISTENT. ALL DIMENSIONS SHALL BE CHECKED AND VERIFIED BY THE CONTRACTOR PRIOR TO ANY COMMENCEMENT OF ANY WORKS ON SITE. TO CLARIFY ANY DISCREPANCIES BETWEEN THE DRAWINGS AND DOCUMENTATION RELEVANT TO THE PROJECT.

2. ALL PLAN DRAWINGS AND DOCUMENTATION RELEVANT TO THE PROJECT SHALL BE KEPT ON SITE AT ALL TIMES.

3. DISPOSAL / SITE WORKS, GROUND LEVELS MAY VARY DUE TO SITE CONDITIONS.

4. - COPYRIGHT -

5. ALL DRAWINGS REMAIN THE PROPERTY OF PETER PERRAS, ENGINEER OF PERRAS DESIGN GROUP PVT. LTD.

6. NO PART OF THIS DRAWING OR ANY INFORMATION CONTAINED HEREIN MAY BE REPRODUCED OR TRANSMITTED IN ANY FORM OR BY ANY MEANS, ELECTRONIC OR MECHANICAL, WITHOUT WRITTEN CONSENT.

|               |         |
|---------------|---------|
| DRAWN         | M.P     |
| DATE          | JULY.26 |
| CHECKED       | P.PERRA |
| SCALE         | N/A     |
| JOB NUMBER    | 2684    |
| NUMBER IN SET | 7       |
| ISSUE         | A       |

[illegible]

IMPORTANT NOTE:  
ALL DIMENSIONS AND NOTES ON ALL PLANS MUST BE CHECKED AND VERIFIED BY BUILDER AND/OR OWNER PRIOR TO COMMENCEMENT OF ANY BUILDING WORKS TO CLARIFY AND CONFIRM WITH PERRAS DESIGN GROUP ANY DISCREPANCIES ON ALL DOCUMENTS AND PLANS PROVIDED FOR CONSTRUCTION. ANY WORK INDICATED ON THE PLAN BUT NOT IN THE SPECIFICATION OR VICE VERSA, AND ANY ITEM NOT SHOWN IN EITHER PLAN OR SPECIFICATION BUT WHICH IS INDICATED IN THE COORDINATE OF THE PROPOSED CONSTRUCTION, OR OTHERWISE TO BE DONE AS PART OF THE CONTRACT, VIOLATION TO PLANS SPECIFICATIONS MAY NOT BE MADE WITHOUT WRITTEN CONSENT OF THE OWNER. IT IS THE RESPONSIBILITY OF THE BUILDER/ENGINEER TO VERIFY PLANS AND SPECIFICATIONS AS TO THEIR ACCURACY AND SUFFICIENCY AND ALL SITE WORKS MUST COMPLY WITH CURRENT BCA AND AUSTRALIAN STANDARDS

## BASIX™Certificate

Building Sustainability Index  
www.planningportal.nsw.gov.au/development-and-assessment/basix

### Single Dwelling

Certificate number: 15583635

This certificate confirms that the proposed development will meet the NSW government's requirements for sustainability, if it is built in accordance with the commitments set out below. Terms used in this certificate, or in the commitments, have the meaning given by the document entitled "BASIX Definitions" dated 10/09/2020 published by the Department. This document is available at www.planningportal.nsw.gov.au/definitions

Secretary  
Date of issue: Wednesday, 29 July 2026  
To be valid, this certificate must be submitted with a development application or lodged with a complying development certificate application within 3 months of the date of issue.



| Project summary                                |                                |             |
|------------------------------------------------|--------------------------------|-------------|
| Project name                                   | 6 AITAPE PLACE HOLSWORTHY - GF |             |
| Street address                                 | 6 AITAPE Place HOLSWORTHY 2173 |             |
| Local Government Area                          | Liverpool City Council         |             |
| Plan type and plan number                      | Deposited Plan DP235683        |             |
| Lot no.                                        | 339                            |             |
| Section no.                                    | -                              |             |
| Project type                                   | dwelling house (detached)      |             |
| No. of bedrooms                                | 2                              |             |
| Project score                                  |                                |             |
| Water                                          | ✔ 40                           | Target 40   |
| Thermal Performance<br>(Do-it-Yourself Method) | ✔ Pass                         | Target Pass |
| Energy                                         | ✔ 67                           | Target 66   |
| Materials                                      | ✔ 44                           | Target n/a  |

| Certificate Prepared by |                   |  |
|-------------------------|-------------------|--|
| Name / Company Name     | Five Star NATHERS |  |
| ABN (if applicable)     | 25033080585       |  |

BASIX Department of Planning, Housing and Infrastructure www.basix.nsw.gov.au Version: 4.04 / EUCALYPTUS\_03\_01\_0 Certificate No.: 15583635 Wednesday, 29 July 2026 page 1/11

| Thermal Performance and Materials commitments   |  |  |  | Show on DA plans | Show on CC/CDC plans & specs | Certifier check |
|---|--|--|--|------------------|------------------------------|-----------------|
| Do-it-yourself Method   |  |  |  |                  |                              |                 |
| General features   |  |  |  |                  |                              |                 |
| The dwelling must be a Class 1 dwelling according to the National Construction Code, and must not have more than 2 storeys.                                          |  |  |  | ✓                | ✓                            | ✓               |
| The conditioned floor area of the dwelling must not exceed 300 square metres.                                                                                        |  |  |  | ✓                | ✓                            | ✓               |
| The dwelling must not contain open mezzanine area exceeding 25 square metres.                                                                                        |  |  |  | ✓                | ✓                            | ✓               |
| The dwelling must not contain third level habitable attic room.   |  |  |  | ✓                | ✓                            | ✓               |
| Floor, walls and ceiling/roof   |  |  |  |                  |                              |                 |
| The applicant must construct the floor(s), walls, and ceiling/roof of the dwelling in accordance with the specifications listed in the table below.                  |  |  |  | ✓                | ✓                            | ✓               |
| The applicant must adopt one of the options listed in the tables below to address thermal bridging in metal framed floor(s), walls and ceiling/roof of the dwelling. |  |  |  | ✓                | ✓                            | ✓               |
| The applicant must show through receipts that the materials purchased for construction are consistent with the specifications listed in the tables below.            |  |  |  |                  |                              | ✓               |

| Construction                                                     | Area - m²          | Additional insulation required                               | Options to address thermal bridging | Other specifications                         |
|------------------------------------------------------------------|--------------------|--------------------------------------------------------------|-------------------------------------|----------------------------------------------|
| Floor - concrete slab on ground, conventional slab.              | 52.7               | nil/not specified                                            | nil                                 |                                              |
| external wall: AAC veneer, frame: timber - untreated softwood.   | all external walls | 1.88 (or 3.00 including construction)/Rogelass batts or roll | nil                                 | wall colour: Light (solar absorbance < 0.48) |
| external garage wall: cavity brick, frame: no frame.             | 39.5               | none                                                         | nil                                 |                                              |
| internal wall: plasterboard, frame: timber - untreated softwood. | 29                 | none                                                         | nil                                 |                                              |

BASIX Department of Planning, Housing and Infrastructure www.basix.nsw.gov.au Version: 4.04 / EUCALYPTUS\_03\_01\_0 Certificate No.: 15583635 Wednesday, 29 July 2026 page 4/11

| Thermal Performance and Materials commitments   |  |  |  | Show on DA plans | Show on CC/CDC plans & specs | Certifier check |
|---|--|--|--|------------------|------------------------------|-----------------|
| Glazed windows, doors and skylights   |  |  |  |                  |                              |                 |
| The applicant must install the windows, glazed doors and shading devices described in the table below, in accordance with the specifications listed in the table. Relevant overshadowing specifications must be satisfied for each glazed window and door.                                                                                      |  |  |  | ✓                | ✓                            | ✓               |
| The dwelling may have 1 skylight (<0.7 square metres) which is not listed in the table.   |  |  |  | ✓                | ✓                            | ✓               |
| The following requirements must also be satisfied in relation to each window and glazed door:   |  |  |  | ✓                | ✓                            | ✓               |
| • The applicant must install windows and glazed doors in accordance with the height and width, frame and glazing types listed in the table.   |  |  |  | ✓                | ✓                            | ✓               |
| • Each window and glazed door must have a U-value no greater than that listed and a Solar Heat Gain Coefficient (SHGC) within the range listed. Total system U values and SHGC must be calculated in accordance with National Fenestration Rating Council (NFRC) conditions.                                                                    |  |  |  | ✓                | ✓                            | ✓               |
| The applicant must install the skylights described in the table below, in accordance with the specifications listed in the table. Total skylight area must not exceed 2 square metres (the 3 square metre limit does not include the optional additional skylight of less than 0.7 square metres that does not have to be listed in the table). |  |  |  | ✓                | ✓                            | ✓               |

| Glazed window/door no. | Maximum height (mm) | Maximum width (mm) | Frame and glass specification                              | Shading device (Dimension within 10%)                    | Overshadowing    |
|------------------------|---------------------|--------------------|------------------------------------------------------------|----------------------------------------------------------|------------------|
| North facing           |                     |                    |                                                            |                                                          |                  |
| W18                    | 900.00              | 600.00             | aluminium, single glazed (U-value <=7.5, SHGC 0.74 - 0.90) | none                                                     | not overshadowed |
| South facing           |                     |                    |                                                            |                                                          |                  |
| S03                    | 2400.00             | 2400.00            | aluminium, single glazed (U-value <=3.5, SHGC 0.33 - 0.40) | eaves 900 mm, 200 mm above head of window or glazed door | not overshadowed |
| W21                    | 1200.00             | 1800.00            | aluminium, single glazed (U-value <=7.5, SHGC 0.74 - 0.90) | eaves 900 mm, 200 mm above head of window or glazed door | not overshadowed |
| West facing            |                     |                    |                                                            |                                                          |                  |

BASIX Department of Planning, Housing and Infrastructure www.basix.nsw.gov.au Version: 4.04 / EUCALYPTUS\_03\_01\_0 Certificate No.: 15583635 Wednesday, 29 July 2026 page 7/11

| Energy Commitments                                                                                                   |  |  | Show on DA plans | Show on CC/CDC plans & specs | Certifier check |
|---|--|--|------------------|------------------------------|-----------------|
| The applicant must install a window and/or skylight in 1 bathroom/toilet(s) in the development for natural lighting. |  |  | ✓                | ✓                            | ✓               |
| Other   |  |  |                  |                              |                 |
| The applicant must install a gas cooktop & electric oven in the kitchen of the dwelling.                             |  |  |                  | ✓                            |                 |

BASIX Department of Planning, Housing and Infrastructure www.basix.nsw.gov.au Version: 4.04 / EUCALYPTUS\_03\_01\_0 Certificate No.: 15583635 Wednesday, 29 July 2026 page 10/11

## Description of project

| Project address                         |                                |
|-----------------------------------------|--------------------------------|
| Project name                            | 6 AITAPE PLACE HOLSWORTHY - GF |
| Street address                          | 6 AITAPE Place HOLSWORTHY 2173 |
| Local Government Area                   | Liverpool City Council         |
| Plan type and plan number               | Deposited Plan DP235683        |
| Lot no.                                 | 339                            |
| Section no.                             | -                              |
| Project type                            |                                |
| Project type                            | dwelling house (detached)      |
| No. of bedrooms                         | 2                              |
| Site details                            |                                |
| Site area (m²)                          | 771                            |
| Roof area (m²)                          | 72                             |
| Conditioned floor area (m²)             | 55.4                           |
| Unconditioned floor area (m²)           | 4.59                           |
| Total area of garden and lawn (m²)      | 60                             |
| Roof area of the existing dwelling (m²) | 0                              |

| Assessor details and thermal loads                  |        |             |  |
|-----------------------------------------------------|--------|-------------|--|
| NATHERS assessor number                             | n/a    |             |  |
| NATHERS certificate number                          | n/a    |             |  |
| Climate zone                                        | n/a    |             |  |
| Area adjusted cooling load (MJ/m <sup>2</sup> year) | n/a    |             |  |
| Area adjusted heating load (MJ/m <sup>2</sup> year) | n/a    |             |  |
| Project score                                       |        |             |  |
| Water                                               | ✓ 40   | Target 40   |  |
| Thermal Performance (Do-it-Yourself Method)         | ✓ Pass | Target Pass |  |
| Energy                                              | ✓ 67   | Target 66   |  |
| Materials                                           | ✓ 64   | Target n/a  |  |

BASIX Department of Planning, Housing and Infrastructure www.basix.nsw.gov.au Version: 4.04 / EUCALYPTUS\_03\_01\_0 Certificate No.: 15583635 Wednesday, 29 July 2026 page 3/11

| Construction                                                                                      | Area - m²   | Additional insulation required                                                           | Options to address thermal bridging | Other specifications                                                                                               |
|---------------------------------------------------------------------------------------------------|---|------------------------------------------------------------------------------------------|-------------------------------------|---|
| ceiling and roof - flat ceiling / pitched roof, framed - metal roof, timber - untreated softwood. | 72   | ceiling: 3.5 (up), roof: full batts; ceiling: Rongelass batts or nil; roof: fullbarking. | nil                                 | roof space ventilation: unventilated; roof colour: medium (solar absorbance 0.6-0.7); ceiling area fully insulated |
| Note                                                                                              | • Insulation specified in this Certificate must be installed in accordance with the ABCB Housing Provisions (Part 13.2.2) of the National Construction Code.                     |                                                                                          |                                     |   |
| Note                                                                                              | • If the additional ceiling insulation listed in the table above is greater than R3.5, refer to the ABCB Housing Provisions (Part 13.2.3 (b)) of the National Construction Code. |                                                                                          |                                     |   |
| Note                                                                                              | • In some climate zones, insulation should be installed with due consideration of contamination and associated interaction with adjoining building materials.                    |                                                                                          |                                     |   |
| Note                                                                                              | • Thermal breaks must be installed in metal framed walls and applicable roofs in accordance with the ABCB Housing Provisions of the National Construction Code.                  |                                                                                          |                                     |   |

BASIX Department of Planning, Housing and Infrastructure www.basix.nsw.gov.au Version: 4.04 / EUCALYPTUS\_03\_01\_0 Certificate No.: 15583635 Wednesday, 29 July 2026 page 8/11

| Glazed window/door no. | Maximum height (mm) | Maximum width (mm) | Frame and glass specification                              | Shading device (Dimension within 10%)                                | Overshadowing    |
|------------------------|---------------------|--------------------|------------------------------------------------------------|----------------------------------------------------------------------|------------------|
| W20                    | 1000.00             | 1200.00            | aluminium, single glazed (U-value <=7.5, SHGC 0.74 - 0.90) | eaving (adjustable) 500 mm, 0 mm above base of window or glazed door | not overshadowed |
| W19                    | 1800.00             | 1200.00            | aluminium, single glazed (U-value <=7.5, SHGC 0.74 - 0.90) | eaving (adjustable) 500 mm, 0 mm above base of window or glazed door | not overshadowed |

BASIX Department of Planning, Housing and Infrastructure www.basix.nsw.gov.au Version: 4.04 / EUCALYPTUS\_03\_01\_0 Certificate No.: 15583635 Wednesday, 29 July 2026 page 8/11

| Legend   |  |
|---|--|
| In these commitments, "applicant" means the person carrying out the development.   |  |
| Commitments identified with a ✓ in the "Show on DA plans" column must be shown on the plans accompanying the development application for the proposed development (if a development application is to be lodged for the proposed development).             |  |
| Commitments identified with a ✓ in the "Show on CC/CDC plans and specs" column must be shown in the plans and specifications accompanying the application for a construction certificate / complying development certificate for the proposed development. |  |
| Commitments identified with a ✓ in the "Certifier check" column must be certified by a certifying authority as having been fulfilled, before a final occupation certificate (either interim or final) for the development may be issued.                   |  |

BASIX Department of Planning, Housing and Infrastructure www.basix.nsw.gov.au Version: 4.04 / EUCALYPTUS\_03\_01\_0 Certificate No.: 15583635 Wednesday, 29 July 2026 page 11/11

### Schedule of BASIX commitments

The commitments set out below regulate how the proposed development is to be carried out. It is a condition of any development consent granted, or complying development certificate issued, for the proposed development, that BASIX commitments be complied with.

| Water Commitments   |  |  |  | Show on DA plans | Show on CC/CDC plans & specs | Certifier check |
|---|--|--|--|------------------|------------------------------|-----------------|
| Fixtures   |  |  |  |                  |                              |                 |
| The applicant must install showerheads with a minimum rating of 5 star (> 4.5 but <= 6 L/min plus spray force and/or coverage tests) in all showers in the development.                                                        |  |  |  |                  | ✓                            | ✓               |
| The applicant must install a toilet flushing system with a minimum rating of 4 star in each toilet in the development.   |  |  |  |                  | ✓                            | ✓               |
| The applicant must install taps with a minimum rating of 5 star in the kitchen in the development.   |  |  |  |                  | ✓                            |                 |
| The applicant must install basin taps with a minimum rating of 5 star in each bathroom in the development.   |  |  |  |                  | ✓                            |                 |
| Alternative water   |  |  |  |                  |                              |                 |
| Rainwater tank   |  |  |  |                  |                              |                 |
| The applicant must install a rainwater tank of at least 1800 litres on the site. This rainwater tank must meet, and be installed in accordance with, the requirements of all applicable regulatory authorities.                |  |  |  | ✓                | ✓                            | ✓               |
| The applicant must configure the rainwater tank to collect rain runoff from at least 72 square metres of the roof area of the development (excluding the area of the roof which drains to any stormwater tank or private dam). |  |  |  |                  | ✓                            | ✓               |
| The applicant must connect the rainwater tank to:   |  |  |  |                  |                              |                 |
| • all toilets in the development   |  |  |  |                  | ✓                            | ✓               |
| • at least one outdoor tap in the development (Note: NSW Health does not recommend that rainwater be used for human consumption in areas with potable water supply.)                                                           |  |  |  |                  | ✓                            | ✓               |

BASIX Department of Planning, Housing and Infrastructure www.basix.nsw.gov.au Version: 4.04 / EUCALYPTUS\_03\_01\_0 Certificate No.: 15583635 Wednesday, 29 July 2026 page 3/11

| Thermal Performance and Materials commitments   |  |  |  | Show on DA plans | Show on CC/CDC plans & specs | Certifier check |
|---|--|--|--|------------------|------------------------------|-----------------|
| Ceiling fans   |  |  |  |                  |                              |                 |
| The applicant must install at least one ceiling fan in at least one daytime habitable space, such as living room.                                                                                |  |  |  | ✓                | ✓                            | ✓               |
| • The minimum number and diameter of ceiling fans in a daytime habitable space must be installed in accordance with the ABCB Housing Provisions (Part 13.5.2) of the National Construction Code. |  |  |  | ✓                | ✓                            | ✓               |

BASIX Department of Planning, Housing and Infrastructure www.basix.nsw.gov.au Version: 4.04 / EUCALYPTUS\_03\_01\_0 Certificate No.: 15583635 Wednesday, 29 July 2026 page 8/11

| Energy Commitments   |  |  |  | Show on DA plans | Show on CC/CDC plans & specs | Certifier check |
|---|--|--|--|------------------|------------------------------|-----------------|
| Hot water   |  |  |  |                  |                              |                 |
| The applicant must install the following hot water system in the development, or a system with a higher energy rating: gas instantaneous with a performance of 5 stars.                         |  |  |  | ✓                | ✓                            | ✓               |
| Cooling system   |  |  |  |                  |                              |                 |
| The applicant must install the following cooling system, or a system with a higher energy rating, in at least 1 living area: 1-phase airconditioning - non ducted; Energy rating: EER 2.5 - 3.0 |  |  |  |                  | ✓                            | ✓               |
| The applicant must install the following cooling system, or a system with a higher energy rating, in at least 1 bedroom: 1-phase airconditioning - non ducted; Energy rating: EER 2.5 - 3.0     |  |  |  |                  | ✓                            | ✓               |
| Heating system   |  |  |  |                  |                              |                 |
| The applicant must install the following heating system, or a system with a higher energy rating, in at least 1 living area: 1-phase airconditioning - non ducted; Energy rating: EER 2.5 - 3.0 |  |  |  |                  | ✓                            | ✓               |
| The applicant must install the following heating system, or a system with a higher energy rating, in at least 1 bedroom: 1-phase airconditioning - non ducted; Energy rating: EER 2.5 - 3.0     |  |  |  |                  | ✓                            | ✓               |
| Ventilation   |  |  |  |                  |                              |                 |
| The applicant must install the following exhaust systems in the development:   |  |  |  |                  |                              |                 |
| At least 1 Bathroom: individual fan, ducted to terrace; Operation control: manual switch on/off                                                                                                 |  |  |  |                  | ✓                            | ✓               |
| Kitchen: individual fan, ducted to terrace; Operation control: manual switch on/off   |  |  |  |                  | ✓                            | ✓               |
| Laundry: natural ventilation only, or no laundry; Operation control: n/a   |  |  |  |                  | ✓                            | ✓               |
| Artificial lighting   |  |  |  |                  |                              |                 |
| The applicant must ensure that a minimum of 80% of light fixtures are fitted with fluorescent, compact fluorescent, or light-emitting diode (LED) lamps.                                        |  |  |  |                  | ✓                            | ✓               |
| Natural lighting   |  |  |  |                  |                              |                 |
| The applicant must install a window and/or skylight in the kitchen of the dwelling for natural lighting.                                                                                        |  |  |  | ✓                | ✓                            | ✓               |

BASIX Department of Planning, Housing and Infrastructure www.basix.nsw.gov.au Version: 4.04 / EUCALYPTUS\_03\_01\_0 Certificate No.: 15583635 Wednesday, 29 July 2026 page 8/11



Suite 6, 92 Bathurst Street,  
Liverpool NSW 2170  
Office - (02) 8005 1000  
[www.perrasdesigngroup.com.au](http://www.perrasdesigngroup.com.au)  
PETER PERRAS - DIRECTOR - Mobile 0414 507 259  
Registered Design Practitioner Body Corporate DEP0003999  
Registered Design Practitioner DEP0001985 (All Classes)  
Accredited BDA Aust 6639  
M.BDAA 7488.21



JOB DESCRIPTION  
DEMOLITION AND PROPOSED ALTERATION AND ADDITION TO EXISTING HOUSE AND PROPOSED DETACHED GRANNY FLAT  
AT  
6 AITAPE PLACE, HOLSWORTHY

DRAWING TITLE  
BASIX COMMENTS-2  
CLIENT DETAILS  
FADI YOUSSEF

GENERAL NOTES  
DO NOT SCALE THE DRAWINGS. READ ALL DIMENSIONS SHOWN. ALL DIMENSIONS, NOTES ON ALL PLANS AND CONSENT DOCUMENTS MUST BE CHECKED AND VERIFIED BY THE CONTRACTOR PRIOR TO ANY COMMENCEMENT OF ANY BUILDING WORKS ON SITE, TO CLARIFY ANY DISCREPANCIES BETWEEN ALL PLAN DRAWINGS AND DOCUMENTATION RELEVANT TO THE PROPOSAL / SITE WORKS. GROUND LEVELS MAY VARY DUE TO SITE CONDITIONS.  
- COPYRIGHT -  
THESE DRAWINGS REMAIN THE PROPERTY OF PETER PERRAS, DIRECTOR OF PERRAS DESIGN GROUP PTY LTD, ABN 35 614 757 550 AND CAN NOT BE ALTERED OR REPRODUCED WITHOUT WRITTEN CONSENT.

| DRAWN         | M,P      | REV | AMENDMENTS     |  | BY  | DATE    |
|---------------|----------|-----|----------------|--|-----|---------|
|               |          | A   | CDC SUBMISSION |  | P,P | JULY.26 |
| DATE          | JULY.26  |     |                |  |     |         |
| CHECKED       | P.PERRAS |     |                |  |     |         |
| SCALE         | N/A      |     |                |  |     |         |
| JOB NUMBER    | 2684     |     |                |  |     |         |
| NUMBER IN SET | 7A       |     |                |  |     |         |
| ISSUE         | A        |     |                |  |     |         |

REPORT NOTE:  
ALL DIMENSIONS AND NOTES ON ALL PLANS MUST BE CHECKED AND VERIFIED BY BUILDER AND/OR OWNER PRIOR TO COMMENCEMENT OF ANY BUILDING WORKS TO CLARIFY AND CONFIRM WITH PERRAS DESIGN GROUP ANY DISCREPANCIES ON ALL DOCUMENTS AND PLANS PROVIDED FOR CONSTRUCTION. ANY WORK INDICATED ON THE PLAN BUT NOT IN THE SPECIFICATION OR VICE VERSA AND ANY ITEM NOT SHOWN IN EITHER PLAN OR SPECIFICATION BUT WHICH IS INDICATED NECESSARY AS PART OF PROPOSED CONSTRUCTION (E.G. STAIRS) IS TO BE DONE AS PART OF THE CONTRACT. VARIATIONS TO PLANS/SPECIFICATIONS MAY NOT BE MADE WITHOUT WRITTEN CONSENT OF THE OWNER IT IS THE RESPONSIBILITY OF THE BUILDER/ENGINEER TO VERIFY PLANS AND SPECIFICATIONS AS TO THEIR ACCURACY AND SUSTAINABILITY AND ALL SITE WORKS MUST COMPLY WITH CURRENT BCA AND AUSTRALIAN STANDARDS

SITE AREA - 771.4m2

SITE CALCULATION


CONTROL:  
GFA ALLOWED = 335SQM

ACHEIVED:

MAIN DWELLING GROUND FLOOR AREA(MINUS 18SQM GARAGE) = 236.67SQM

GRANNY GROUND FLOOR AREA(meassured from external walls) = 60SQM

GROSS FLOOR AREA = 296.67SQM

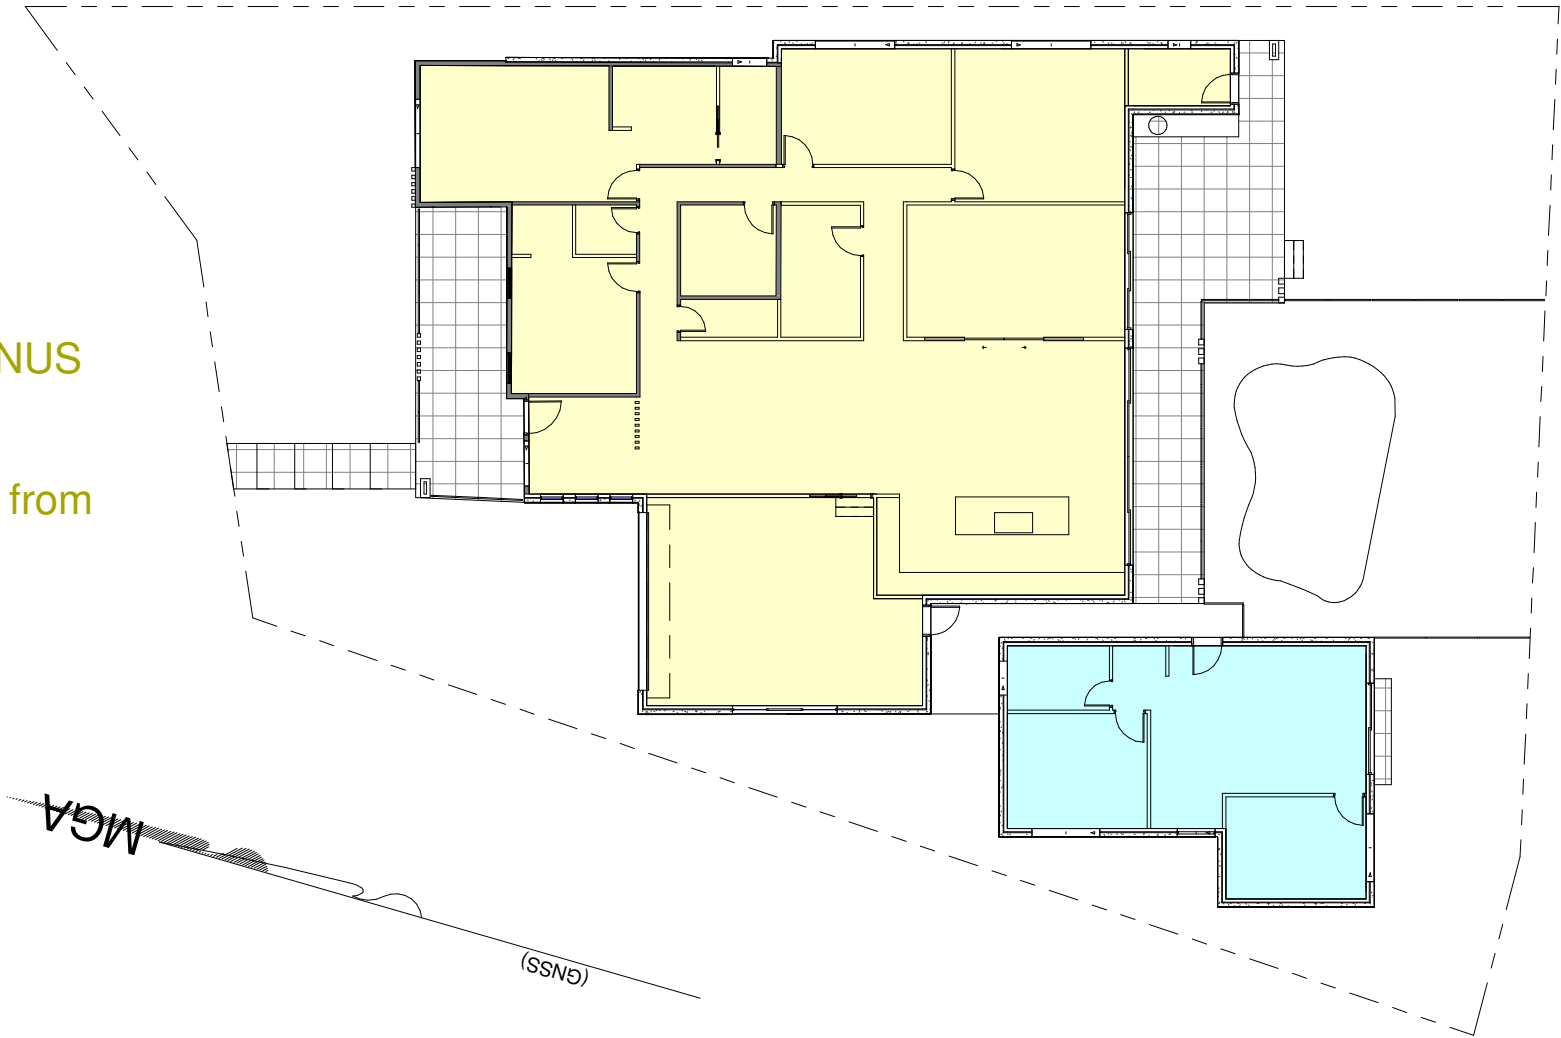

GFA GROUND FLOOR PLAN  
1:100

| State Environmental Planning Policy<br>(Exempt and<br>Complying Development Codes) 2021 |                      |
|-----------------------------------------------------------------------------------------|----------------------|
| BY TITLE: 771.4m²                                                                       | LOT 339<br>DP 235663 |
| <b>SITE AREA</b>                                                                        | <b>771.4QM</b>       |
| <b>ALLOWED -</b>                                                                        |                      |
| LANDSCAPE AREA                                                                          | 192.85SQM            |
| LANDSCAPE AREA BEHIND BUILDING LINE                                                     | 96.43SQM             |
| P.O.S AREA                                                                              | 24.05SQM             |
| TOTAL FLOOR AREA                                                                        | 389.5QM              |
| SITE COVERAGE                                                                           | 385.7SQM             |
| <b>ACHIEVED -</b>                                                                       |                      |
| LANDSCAPE AREA                                                                          | 220.53SQM            |
| LANDSCAPE AREA BEHIND BUILDING LINE                                                     | 140.67SQM            |
| P.O.S AREA                                                                              | 24SQM                |
| EX/PRO GROUND FLOOR AREA (measured from external walls)                                 | 270.36SQM            |
| PRO. GRANNY FLAT FLOOR AREA (measured from external walls)                              | 60SQM                |
| TOTAL FLOOR AREA                                                                        | 330.36SQM            |
| SITE COVERAGE                                                                           | 330.36SQM            |

| State Environmental Planning Policy<br>(Exempt and<br>Complying Development Codes) 2008 |                      |
|-----------------------------------------------------------------------------------------|----------------------|
| BY TITLE: 771.4m²                                                                       | LOT 339<br>DP 235663 |
| <b>SITE AREA</b>                                                                        | <b>771.4QM</b>       |
| <b>ALLOWED -</b>                                                                        |                      |
| LANDSCAPE AREA                                                                          | 231.42SQM            |
| LANDSCAPE AREA BEHIND BUILDING LINE                                                     | 150.94SQM            |
| LANDSCAPE AREA FORWARD BUILDING LINE                                                    | 57.86SQM             |
| P.O.S AREA                                                                              | 24SQM                |
| GROSS FLOOR AREA                                                                        | 335SQM               |
| <b>ACHIEVED -</b>                                                                       |                      |
| LANDSCAPE AREA                                                                          | 239.18SQM            |
| LANDSCAPE AREA BEHIND BUILDING LINE                                                     | 159.32SQM            |
| LANDSCAPE AREA FORWARD BUILDING LINE                                                    | 79.86SQM             |
| P.O.S AREA                                                                              | 24SQM                |
| EX/PROP GROUND FLOOR AREA (measured from internal walls)<br>(minus 18sqm garage)        | 236.67SQM            |
| PROP. GRANNY FLAT AREA (measured from external walls)                                   | 60SQM                |
| GROSS FLOOR AREA(MINUS 18SQM GARAGE)                                                    | 296.67SQM            |



PLANS BY...  
**perras design group**

Suite 6, 92 Bathurst Street,  
Liverpool NSW 2170  
Office - (02) 8005 1000

[www.perrasdesigngroup.com.au](http://www.perrasdesigngroup.com.au)  
PETER PERRAS - DIRECTOR - Mobile 0414 507 259  
Registered Design Practitioner Body Corporate DEP0003999  
Registered Design Practitioner DEP0001985 (All Classes)  
Accredited BDA Aust 6639  
M.BDAA 7488.21



ACCREDITED  
BUILDING DESIGNER

JOB DESCRIPTION

DEMOLITION AND PROPOSED  
ALTERATION AND ADDITION TO  
EXISTING HOUSE AND PROPOSED  
DETACHED GRANNY FLAT

AT  
6 AITAPE PLACE, HOLSWORTHY

DRAWING TITLE

GFA CALCULATIONS & SOFT SOIL  
AREA

CLIENT DETAILS

FADI YOUSSEF

GENERAL NOTES

DO NOT SCALE THE DRAWINGS. READ ALL DIMENSIONS SHOWN.  
ALL DIMENSIONS, NOTES ON ALL PLANS AND CONSENT  
DOCUMENTS MUST BE CHECKED AND VERIFIED BY THE  
CONTRACTOR PRIOR TO ANY COMMENCEMENT OF ANY  
BUILDING WORKS ON SITE, TO CLARIFY ANY DISCREPANCIES  
BETWEEN ALL PLAN DRAWINGS AND DOCUMENTATION RELEVANT  
TO THE PROPOSAL / SITE WORKS. GROUND LEVELS MAY VARY  
DUE TO SITE CONDITIONS.  
- COPYRIGHT -  
THESE DRAWINGS REMAIN THE PROPERTY OF PETER PERRAS,  
DIRECTOR OF PERRAS DESIGN GROUP PTY LTD.  
ABN 35 614 757 550 AND CAN NOT BE ALTERED OR REPRODUCED  
WITHOUT WRITTEN CONSENT.

|               |          |
|---------------|----------|
| DRAWN         | M,P      |
| DATE          | JULY.26  |
| CHECKED       | P.PERRAS |
| SCALE         | N/A100   |
| JOB NUMBER    | 2684     |
| NUMBER IN SET | 8        |
| ISSUE         | A        |

| REV | AMENDMENTS     | BY  | DATE    |
|-----|----------------|-----|---------|
| A   | CDC SUBMISSION | P.P | JULY.26 |
|     |                |     |         |
|     |                |     |         |
## GENERAL NOTES

All off-street car parking spaces and vehicle access must comply with AS/NZS 2890.1:2004, Parking facilities, Part 1: Off-street car parking.  
Part 9.2 – Boundary Wall Notes:  
Boundary Wall to be Fire Rated from footing to underside of roof to comply with NCC & achieve an FRL of 60/60/60  
Part 9.3 – Separating Wall Notes  
Boundary wall from footing to underside of the roof  
Separating wall to achieve a minimum sound insulation of not less than 50 [Rw + Ctr (airborne)]  
Services for separating walls must comply with Part 9.3.2  
Steel and timber beams not to penetrate party wall  
No services within boundary wall  
Part 3.4 – Termite compliance/note on plan  
Part 5.7 – Masonry walls to be weatherproofed  
Part 6.2.1 – Sub-Floor Ventilation  
Part 7.2, H1D7 – Roof pitch – metal sheet roofing 15 degrees  
Part 7.3 H1D7, Roof pitch – tile Roofing 15 degrees  
Part 8.3 – Glazing to comply with AS1288-2006, AS2047-2014, H1D8 of the NCC 2022 & manufacturers technical specification.  
Part 9.2.9(4)(b) – Non-Combustible Eave Lining  
Part 9.3.1(5) – Vertical lining eave separation  
Part 10.2, H2D8 – Waterproofing to comply with NCC 2022 Part 10.2, H2D8, AS 3740, AS 4654.1 and AS 4654.2  
Part 9.5, H3D3 – smoke alarm  
Part 10.3, H4D4 – Habitable room heights, non-habitable room height  
Part 10.4, H5D5, Lift-off hinges clause, wash facilities and washtub  
Part 10.5, H4D6 Natural lighting  
Part 10.6, H4D4 – mechanical ventilation  
Part 10.6 H4D7 – Natural Ventilation  
Part 10.4.2 – Lift-Off Hinges  
Part 11.2 – Stairs  
I. Maximum 18 stair risers without landing  
II. Minimum 2m head height  
Part 11.3.3 – Barriers to prevent falls to comply to be reflected/noted on plans for stairs, voids, balconies, alfresco  
Section H7D2 – Pool Fence Requirements in accordance with AS1926.1-2012:  
I. Windows opening to pool area to be protected (alfresco openings to be protected)  
II. 1.8m Boundary Fence  
III. Appropriate warning sign, including details of resuscitation (CPR) techniques, in the immediate vicinity of the pool area and which can be easily read from a distance of 3 metres  
IV. Metal pool fence spigots to be earthed in accordance with AS/NZS3000:2007 Section 5.6.2.5 & 5.6.2.6  
Part A6 – building classification

## CONDENSATION MANAGEMENT

(1) An exhaust system installed in a kitchen, bathroom, sanitary compartment or laundry must have a minimum flow rate of—  
(a) 25 L/s for a bathroom or sanitary compartment; and  
(b) 40 L/s for a kitchen or laundry.  
(2) Exhaust from a kitchen, kitchen range hood, bathroom, sanitary compartment or laundry must discharge directly or via a shaft or duct to outdoor air.  
(3) Where a venting clothes dryer is installed, it must discharge directly or via a shaft or duct to outdoor air.  
(4) An exhaust system that is not run continuously and is serving a bathroom or sanitary compartment that is not ventilated in accordance with 10.6.2(a) must—  
(a) be interlocked with the room's light switch; and  
(b) include a run-on timer so that the exhaust system continues to operate for 10 minutes after the light switch is turned off.  
(5) Except for rooms that are ventilated in accordance with 10.6.2(a), a room with an exhaust system in accordance with (1) must be provided with make-up air—  
(a) via openings to an adjacent room with a free area of 14,000 mm2; or in accordance with AS 1668.2.

## BUILDING SPECIFICATIONS

The building works included in the subject application will comply with the relevant deemed-to- satisfy provisions of the NCC 2022 National Construction Code (Volume 2- Amendment 2) and relevant standards of construction.

Particular reference is made to the following NCC 2022 provisions and Australian Standards, which form part of the application and will be complied with:

### NCC VOLUME 2 2022

- A. ALL WORKS AND DESIGN IN ACCORDANCE WITH NCC VOLUME 2 2022, MAY EDITION.  
B. PART H1D3 SITE PREPARATION  
C. PART H1D4 FOOTINGS AND SLABS & H1D12 PILED FOOTINGS- FOOTINGS, PIERS, CONCRETE AND SLABS IN ACCORDANCE WITH AS 2870-2011, AS 2159-2009 AND AS 3600-2018,TERMITE PROTECTION TO AS 3660.1-2014  
D. PART H1D5 MASONRY - AS 3700-2018, AS 4773.1-2015 AND AS 4773.2-2015  
E. H PART 1D6 FRAMING - FRAMING SHALL BE IN ACCORDANCE WITH AS 1684.2-2010, AS 1720, AS 4100-2020, AS/NZS 4600-2018, WIND AND LOADING TO AS 1170 PARTS 1-5, AS 4055-2021  
F. PART H1D8 GLAZING - GLAZING AND WINDOWS TO COMPLY WITH AS1288-2021 AND AS 2047-2014  
G. PART H2D2 DRAINAGE – DRAINAGE AND STORMWATER MUST COMPLY WITH AS 3500.3-2021  
H. PART H2D8 EXTERNAL WATERPROOFING - MUST COMPLY WITH AS 4654.1&2-2012  
I. PART H2D5 SUBFLOOR VENTILATION - PART 6.2 OF THE ABCB HOUSING PROVISIONS.  
J. PART H2D6 ROOF AND WALL CLADDING – AS1562.1-2018, AS1562.3-2006 (PLASTIC SHEETS) ROOF TILING: AS 2050. SARKING AS/NZS 4200.1-2017, AAC AS5146.1, EAVES AND FIBRE CEMENT TO COMPLY WITH AS/NZS 2908.2 , HARDBOARD — COMPLY WITH AS/NZS 1859.4-2018, FLASHING TO AS/NZS 2904-1995  
K. PART H3 FIRE SEPARATION - SEPARATING AND EXTERNAL WALLS FRL 60/60/60, SYSTEMS TESTED TO AS 1530.  
L. PART H3D6 SMOKE ALARMS AND EVACUATION LIGHTING – AS 3786-2014, AS 1670.1-2018  
M. PART H4D2 WET AREAS - COMPLIANCE WITH AS 3740-2021  
N. PART H4D4 ROOM HEIGHTS- HABITABLE 2.4M AND NON-HABITABLE 2.1M  
O. PART H4D7 VENTILATION – AS1668.2-2012  
P. PART H4D8 SOUND INSULATION - COMPLIANCE WITH PART 10.7 OF THE ABCB HOUSING PROVISIONS SATISFIES PERFORMANCE REQUIREMENT H4P6 FOR SOUND INSULATION.  
Q. PART H5 SAFE MOVEMENT AND ACCESS – ALL STAIRS, RAMPS, STAIR CONSTRUCTION, BARRIERS, BALUSTRADE, HANDRAILS SHALL COMPLY WITH PART 11.2&3 OF THE ABCB HOUSING PROVISIONS SATISFIES PERFORMANCE REQUIREMENT H5P1 FOR STAIRWAY AND RAMP CONSTRUCTION, DESIGNED TO AS 1170.1. SLIP RESISTANCE TO AS 4586-2013  
R. PART 3.12 ENERGY EFFICIENCY - COMPLY WITH BASIX  
S. PART H7D2 SWIMMING POOLS - SWIMMING POOLS SHALL BE IN ACCORDANCE WITH THE SWIMMING POOL ACT 1992 AND REGULATION 2018. WATER RECIRCULATION SYSTEMS COMPLIES WITH AS 1926.3- 2010, BARRIERS DESIGNED TO AS 1926.1-2012 AND AS 1926.2-2007  
T. PART H7P5 BUILDINGS IN BUSHFIRE PRONE AREAS – CONSTRUCTION AND PLANNING MUST BE TO PLANNING FOR BUSHFIRE PROTECTION 2019 & AS 3959-2018, NASH STANDARD – STEEL FRAMED CONSTRUCTION IN BUSHFIRE AREAS.  
U. PART H7D5 HEATING APPLIANCES, FIREPLACES, CHIMNEYS, AND FLUES - FOR A DOMESTIC SOLID FUEL BURNING APPLIANCE, AS/NZS 2918-2018 OR FOR A HEATING APPLIANCE, PART 12.4 OF THE ABCB HOUSING PROVISIONS.

Demolition: -  
AS 2601(2001) - The demolition of structures

Site Preparation:  
Earthworks - To be carried out in accordance with the requirements of the Environmental Planning & Assessment Act 1979, conditions of development consent and the relevant requirements of Part 3.2 of the ABCB Housing Provisions & H1D3 of NCC 2022 (Volume 2).  
Stormwater drainage - Part H2D2 of NCC 2022 (Volume 2); and ASINZS 3500 (2003) Part 3 - Stormwater drainage  
AS/NZS 3500 (2000) Part 5 - Domestic installations - Section 5 - stormwater drainage Termite protection  
Part 3.4 of ABCB Housing Provisions: and  
AS 3660.1(2000) - Protection of buildings from subterranean termites

Footings and Slabs: -  
Footings and slabs - H1D4 of NCC 2022 (Volume 2); and AS 2870 (2011) - Residential slabs and footings  
AS 3600 (2009) - Concrete structures  
AS 2159 (2009) - Piling - Design and installation  
Site classification - Part A6 of NCC 2022 (Volume 2)

Masonry: -  
Masonry construction - Part H1D5 of NCC 2012 (Volume 2) AS 3700 (2018) - Masonry Structures

Framing: -  
Sub-floor ventilation Part H2D5 of NCC 2022 (Volume 2) Steel framing - Part H1D6 of NCC 2022 (Volume 2)  
Part 6.3 Structural Steel Members of NCC 2022 (Volume 2) and/ or AS 4100 (2020) - Steel structures  
Timber wall, floor and roof framing - H1D6 of ABCB Housing Provisions; and  
AS 1684 (2021) - Residential timber - frame construction  
Part H1 Structure of NCC 2019 (Volume 2) - H1D1 to H1D12  
AS 2918 (2018) - Domestic solid - fuel burning appliances - installation  
Fire Safety - Part 9.1 to 9.5 of ABCB Housing Provisions

Health and amenity: -  
ildings  
Wet areas - Part H4D2 of the NCC 2022 (Volume 2) and AS 3740 (2021) - Waterproofing of wet areas in  
Room heights - Part H4D4 of NCC 2022 (Volume 2)  
Kitchen, sanitary and washing facilities - Part H4D5 of NCC 2022 (Volume 2)  
Natural and artificial light - Part H4D6 of NCC 2022 (Volume 2) Ventilation - Part H4D7 of NCC 2022 (Volume 2)  
Sound insulation - Part H4D8 of NCC 2022 (Volume 2)  
Health and Amenity - Part 10 of ABCB Housing Provisions

Roof and wall cladding: -  
Roof and Wall Cladding - Parts H1D7 of NCC 2022 (Volume 2) and AS 2049 (2002) - Roof files  
Part 7.1 to 7.5 of ABCB Housing Provisions  
Gutters and downpipes - Part 7.4 of ABCB Housing Provisions ; and AS/NZS 3500 (2021)  
Part 3 - Stormwater drainage  
AS/NZS 3500 (2021) - Plumbing & Drainage set (Parts 0-4)

Glazing: -  
Glazing - Part H1D8 of NCC 2022 (Volume 2) AS 1288 (2021) Glass in buildings  
AS 2047 (2047) Windows in buildings Glazing  
Part 8 of the ABCB Housing Provisions

Fire safety:  
Fire Separation - Part 3.7.1 of NCC 2019 (Volume 2)  
Fire Safety - Part H3 of NCC 2022 (Volume 2) - H3D1 to H3D6  
AS 3786 (2023) - Smoke alarms  
AS 2918 (2018) - Domestic solid - fuel burning appliances - installation  
Fire Safety - Part 9.1 to 9.5 of ABCB Housing Provisions

Health and amenity: -  
ildings  
Wet areas - Part H4D2 of the NCC 2022 (Volume 2) and AS 3740 (2021) - Waterproofing of wet areas in  
Room heights - Part H4D4 of NCC 2022 (Volume 2)  
Kitchen, sanitary and washing facilities - Part H4D5 of NCC 2022 (Volume 2)  
Natural and artificial light - Part H4D6 of NCC 2022 (Volume 2) Ventilation - Part H4D7 of NCC 2022 (Volume 2)  
Sound insulation - Part H4D8 of NCC 2022 (Volume 2)  
Health and Amenity - Part 10 of ABCB Housing Provisions  
Safe movement and access:  
Stairway and ramp construction - Part H5D2 of NCC 2022 (Volume 2) Barriers and handrails - Part H5D3 of NCC 2022 (Volume 2)  
Stairway and ramp construction - Part 11.2 of the ABCB Housing Provisions Barriers and handrails - Part 11.3 of the ABCB Housing Provisions

Energy efficiency: -  
Energy Efficiency - Part H6 of the NCC 2022 (Volume 2) Building fabric - Part 13.2 of the ABCB Housing Provisions External glazing - Part 13.3 of the ABCB Housing Provisions  
Building sealing - Part 13.4 of the ABCB Housing Provisions Ceiling fans - Part 13.5 of the ABCB Housing Provisions  
Whole-of-home energy usage - Part 13.6 of the ABCB Housing Provisions Services - Part 13.7 of the ABCB Housing Provisions

Ancillary provisions and additional construction requirements:- Swimming pools - Part H7D2 of the NCC 2022 (Volume 2) Construction in alpine areas - Part H7D3 of the NCC 2022 (Volume 2)  
Construction in bushfire prone areas - Part H7D4 of the NCC 2022 (Volume 2)  
Heating appliances, fireplaces, chimneys and flues - H7D5 of the NCC 2022 (Volume 2) Ancillary Provisions - Part 12 of the ABCB Housing Provisions

Livable housing design:-  
Livable housing design - Part H8 of the NCC 2022 (Volume 2) ABCB Standard for Livable Housing Design

Swimming pool safety: -  
Swimming pool safety fencing I 1992 and Regulation 2018 and AS 1926 Part 1 (2012), Part 2 (2007) & Part 3 (2010)  
Structural design manuals: -  
AS 1170.1 (2002) - Dead and live loads and load combinations AS 1170.2 (2021) or AS 4055 (2021) - Wind loads  
AS 1170.4 (2007) - Earthquake loads  
AS 1720.1 (2010) - Timber structures  
AS 2159 (2009) - Piling - design and installation AS 3600 (2018) - Concrete structures  
AS 4100 (2020) - Steel Structures



PLANS BY...  
**perras design group**

Suite 6, 92 Bathurst Street,  
Liverpool NSW 2170  
Office - (02) 8005 1000

www.perrasdesigngroup.com.au

PETER PERRAS - DIRECTOR - Mobile 0414 507 259

Registered Design Practitioner Body Corporate DEP0003999  
Registered Design Practitioner DEP0001985 (All Classes)  
Accredited BDA Aust 6639  
M.BDAA 7488.21



ACCREDITED  
BUILDING DESIGNER

| JOB DESCRIPTION                                                                                     | DRAWING TITLE                    |
|---|----------------------------------|
| DEMOLITION AND PROPOSED ALTERATION AND ADDITION TO EXISTING HOUSE AND PROPOSED DETACHED GRANNY FLAT | SPECIFICATIONS AND GENERAL NOTES |
| AT<br>6 AITAPE PLACE, HOLSWORTHY                                                                    | CLIENT DETAILS                   |
|   | FADI YOUSSEF                     |

| GENERAL NOTES   |  | DRAWN         | M,P      | REV | AMENDMENTS     |  | BY  | DATE    |
|---|--|---------------|----------|-----|----------------|--|-----|---------|
| DO NOT SCALE THE DRAWINGS. READ ALL DIMENSIONS SHOWN. ALL DIMENSIONS, NOTES ON ALL PLANS AND CONSENT DOCUMENTS MUST BE CHECKED AND VERIFIED BY THE CONTRACTOR PRIOR TO ANY COMMENCEMENT OF ANY BUILDING WORKS ON SITE. TO CLARIFY ANY DISCREPANCIES BETWEEN ALL PLAN DRAWINGS AND DOCUMENTATION RELEVANT TO THE PROPOSAL / SITE WORKS, GROUND LEVELS, MAY VARY DUE TO SITE CONDITIONS.<br><br>THESE DRAWINGS REMAIN THE PROPERTY OF PETER PERRAS, DIRECTOR OF PERRAS DESIGN GROUP PTY LTD. ABN 35 614 757 550 AND CAN NOT BE ALTERED OR REPRODUCED WITHOUT WRITTEN CONSENT. |  | DATE          | JULY.26  | A   | CDC SUBMISSION |  | P,P | JULY.26 |
|   |  | CHECKED       | P.PERRAS |     |                |  |     |         |
|   |  | SCALE         | N/A      |     |                |  |     |         |
|   |  | JOB NUMBER    | 2684     |     |                |  |     |         |
|   |  | NUMBER IN SET | 10       |     |                |  |     |         |
|   |  | ISSUE         | A        |     |                |  |     |         |

**perras** design group

Accredited BDA Aust 6639  
M.BDAA 7488.21

**ACCREDITED**  
**BUILDING DESIGNER**

A detailed cross-section diagram of a balcony assembly. The diagram shows the following layers from top to bottom: a 20mm chipboard/plywood layer, a linear wet-dry tile flooring on a waterproofing adhesive layer, a tile grout layer, and a 15mm plywood layer. The assembly is supported by a concrete slab. On the left, a window frame is shown with a 20mm chipboard/plywood layer. On the right, a door frame is shown with a 20mm chipboard/plywood layer. The diagram is labeled 'BALCONY SECTION' and 'NOT TO SCALE'.

The left diagram shows a transition from a SHOWER area to a BATHROOM AREA. In the shower area, there is a frame-less glass shower screen over a stainless steel trench grate, which sits on a stainless steel continuous grate. Below this is a secondary waterproofing membrane over screed, followed by a primary waterproofing membrane. A 20 mm gap is indicated between the grate assembly and the wall. The floor level is marked as Min. 1.80 Falls. At the threshold, a flexible sealant and a bond breaker (fillet) are used. The right diagram shows a transition from a BATHROOM AREA to another BATHROOM AREA. It features a floor waste opening with a 46 mm depth. The floor level is marked as Min. 1.100 Falls on both sides.

NOTES:

- 1.Sub-sill is installed before door.
- 2.Seal between sill, packer and membrane before drilling fixing holes.