




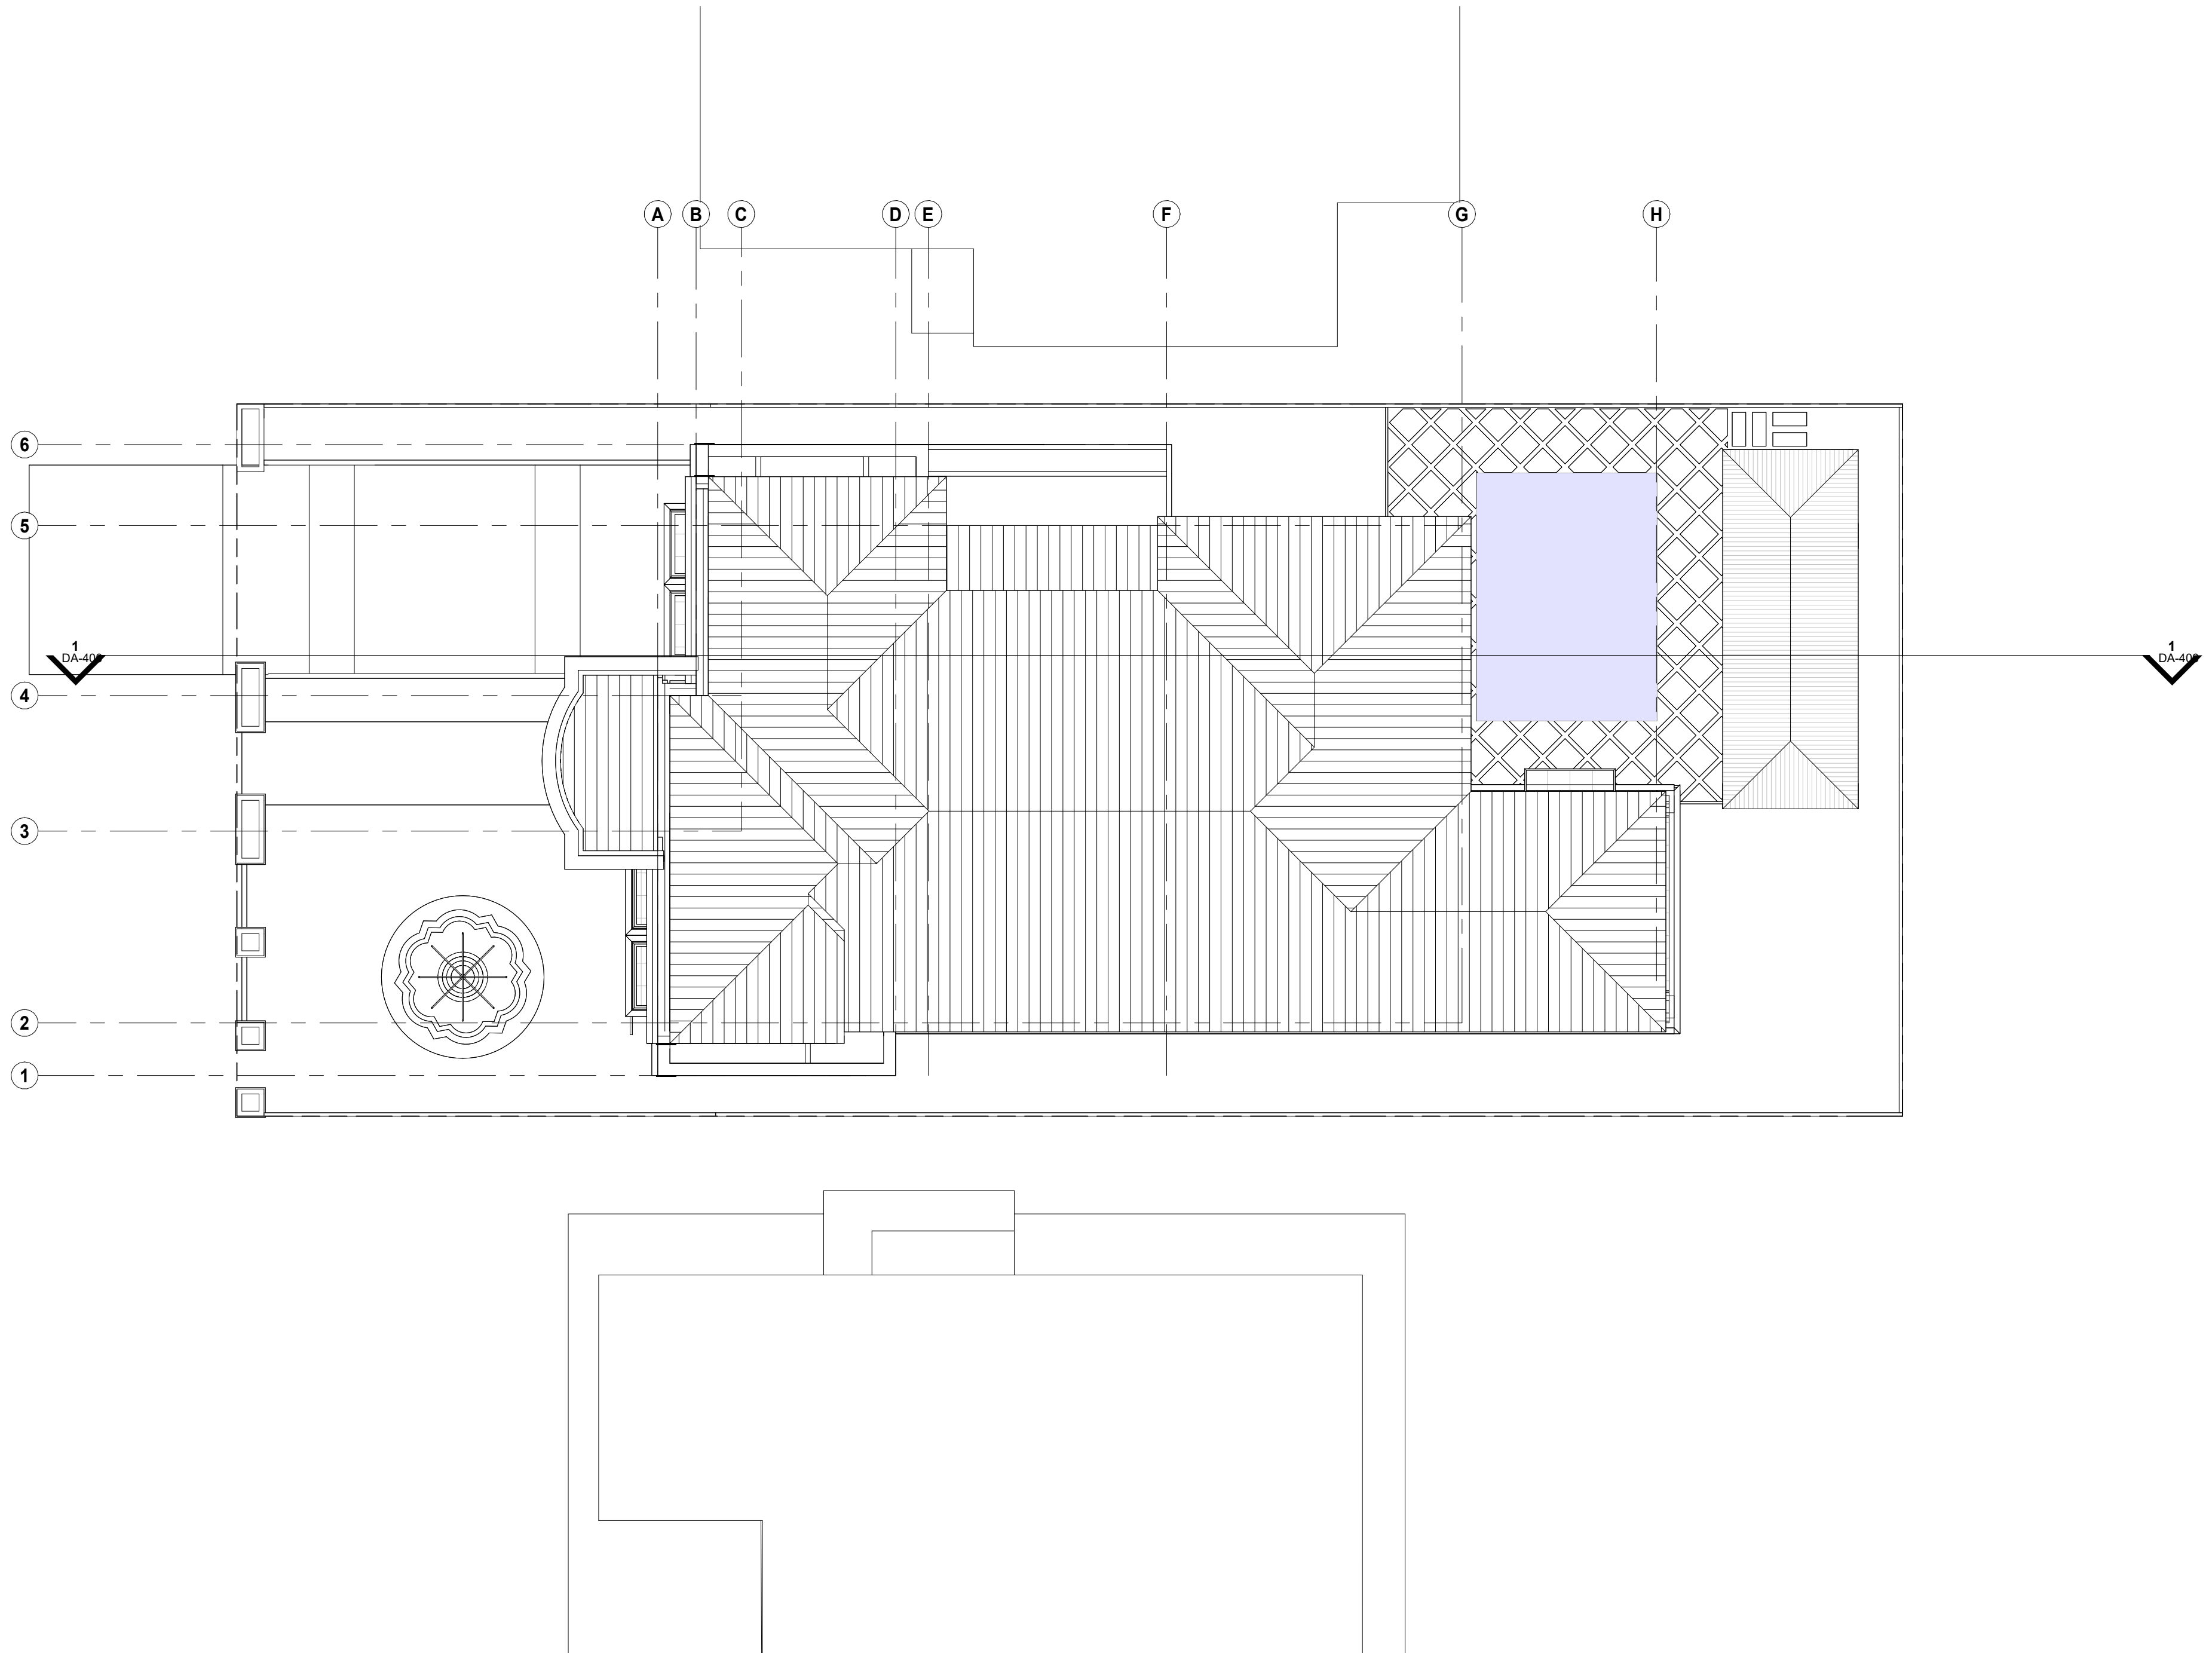


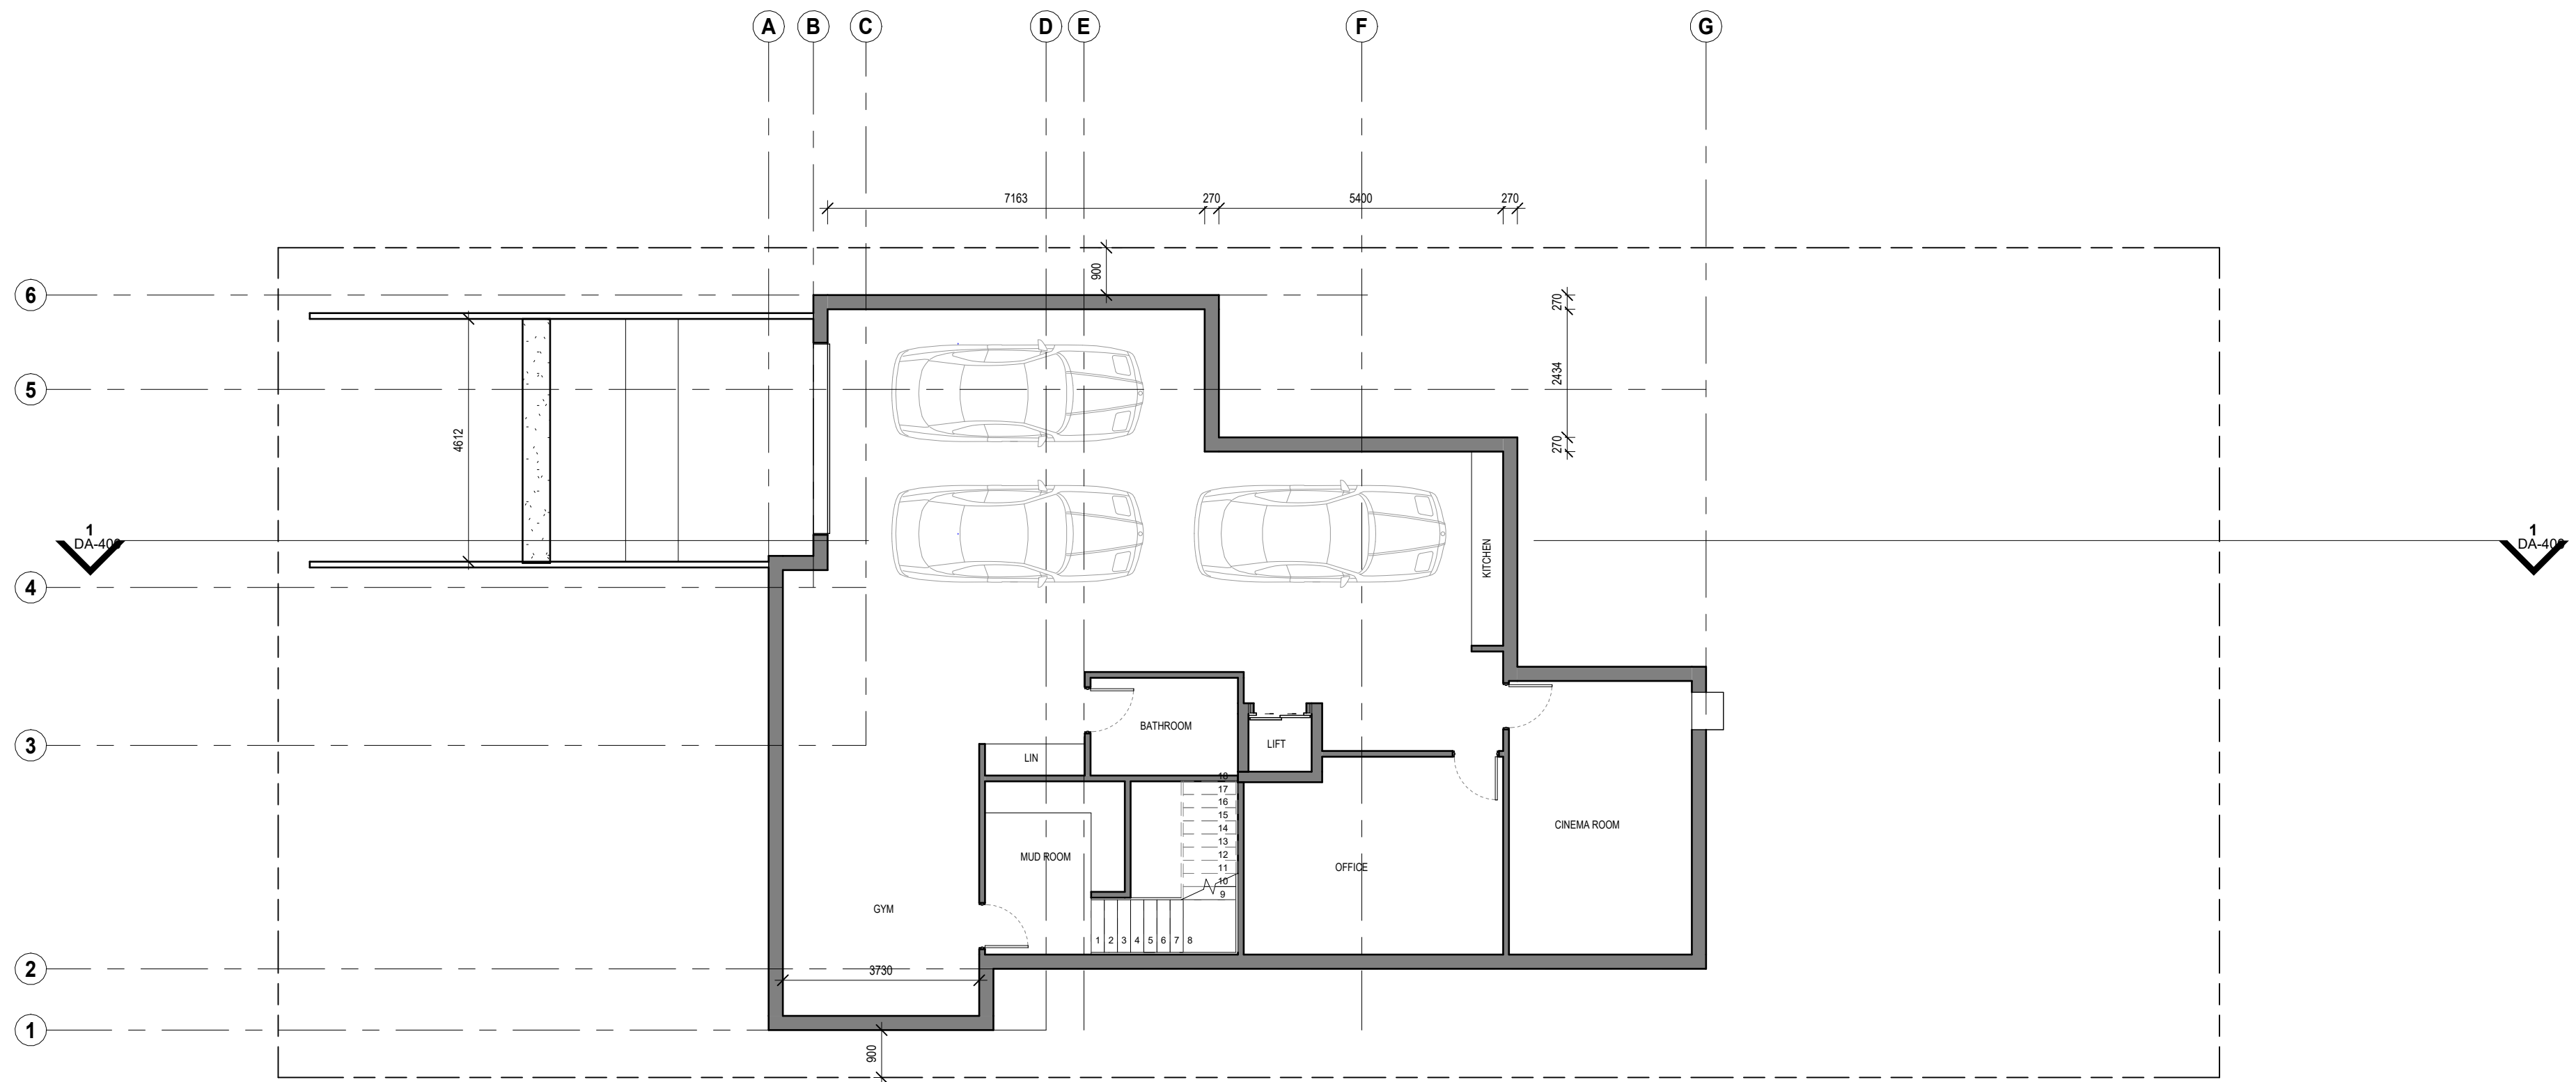


1 01 BASEMENT
1 : 100

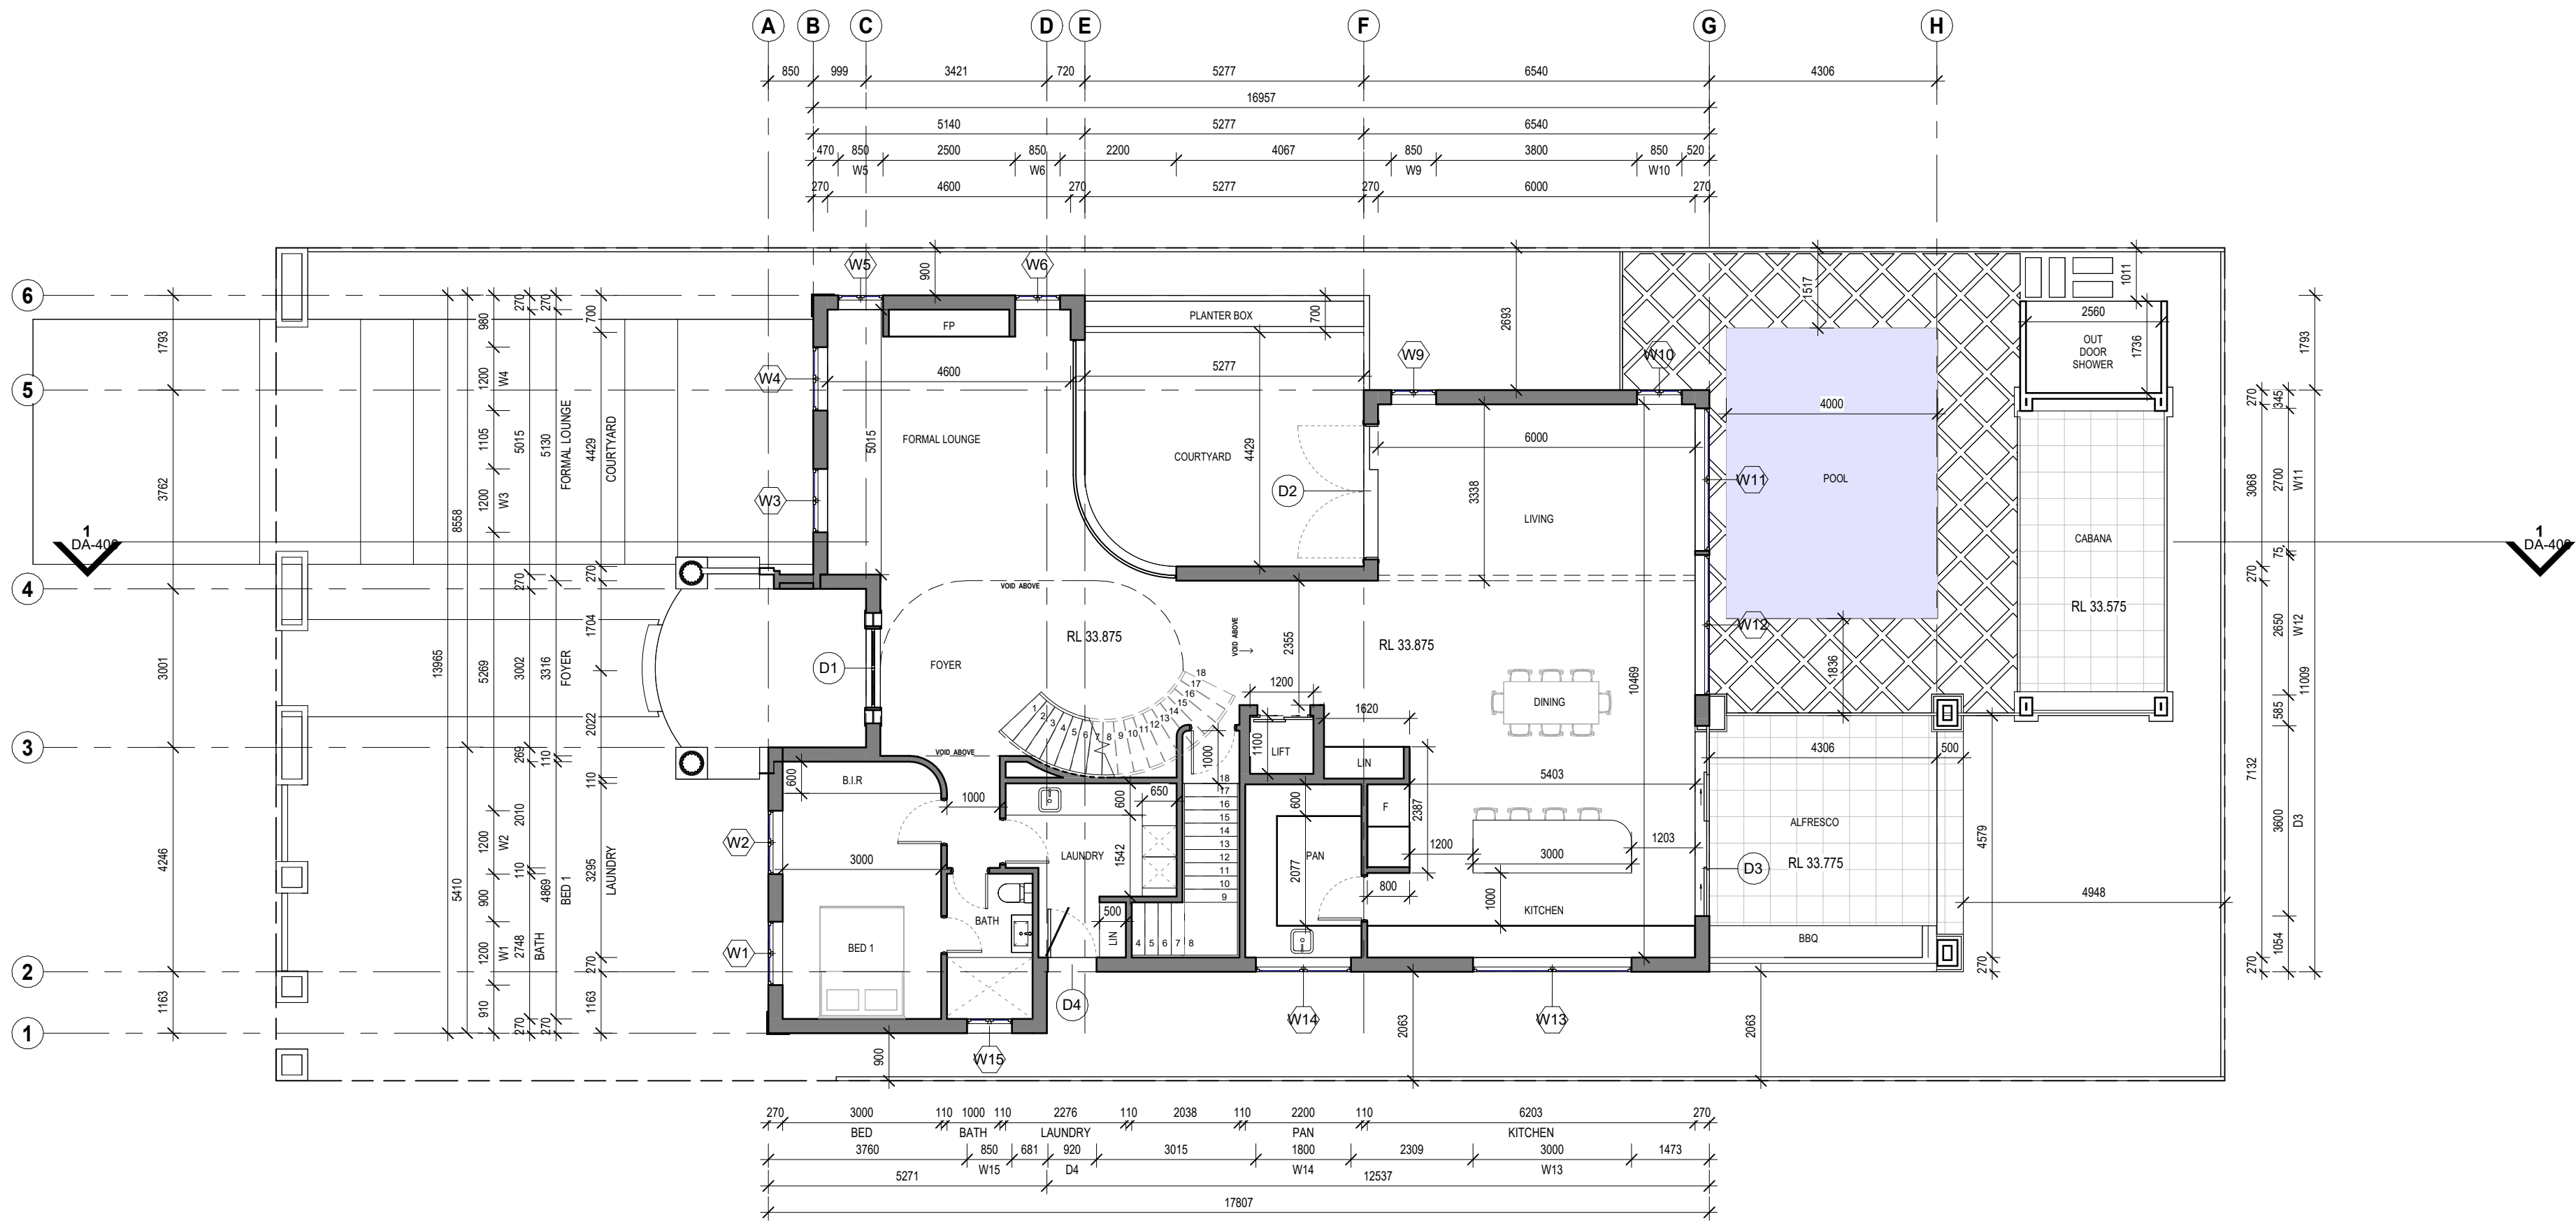


1 03 GROUND FLOOR
1 : 100

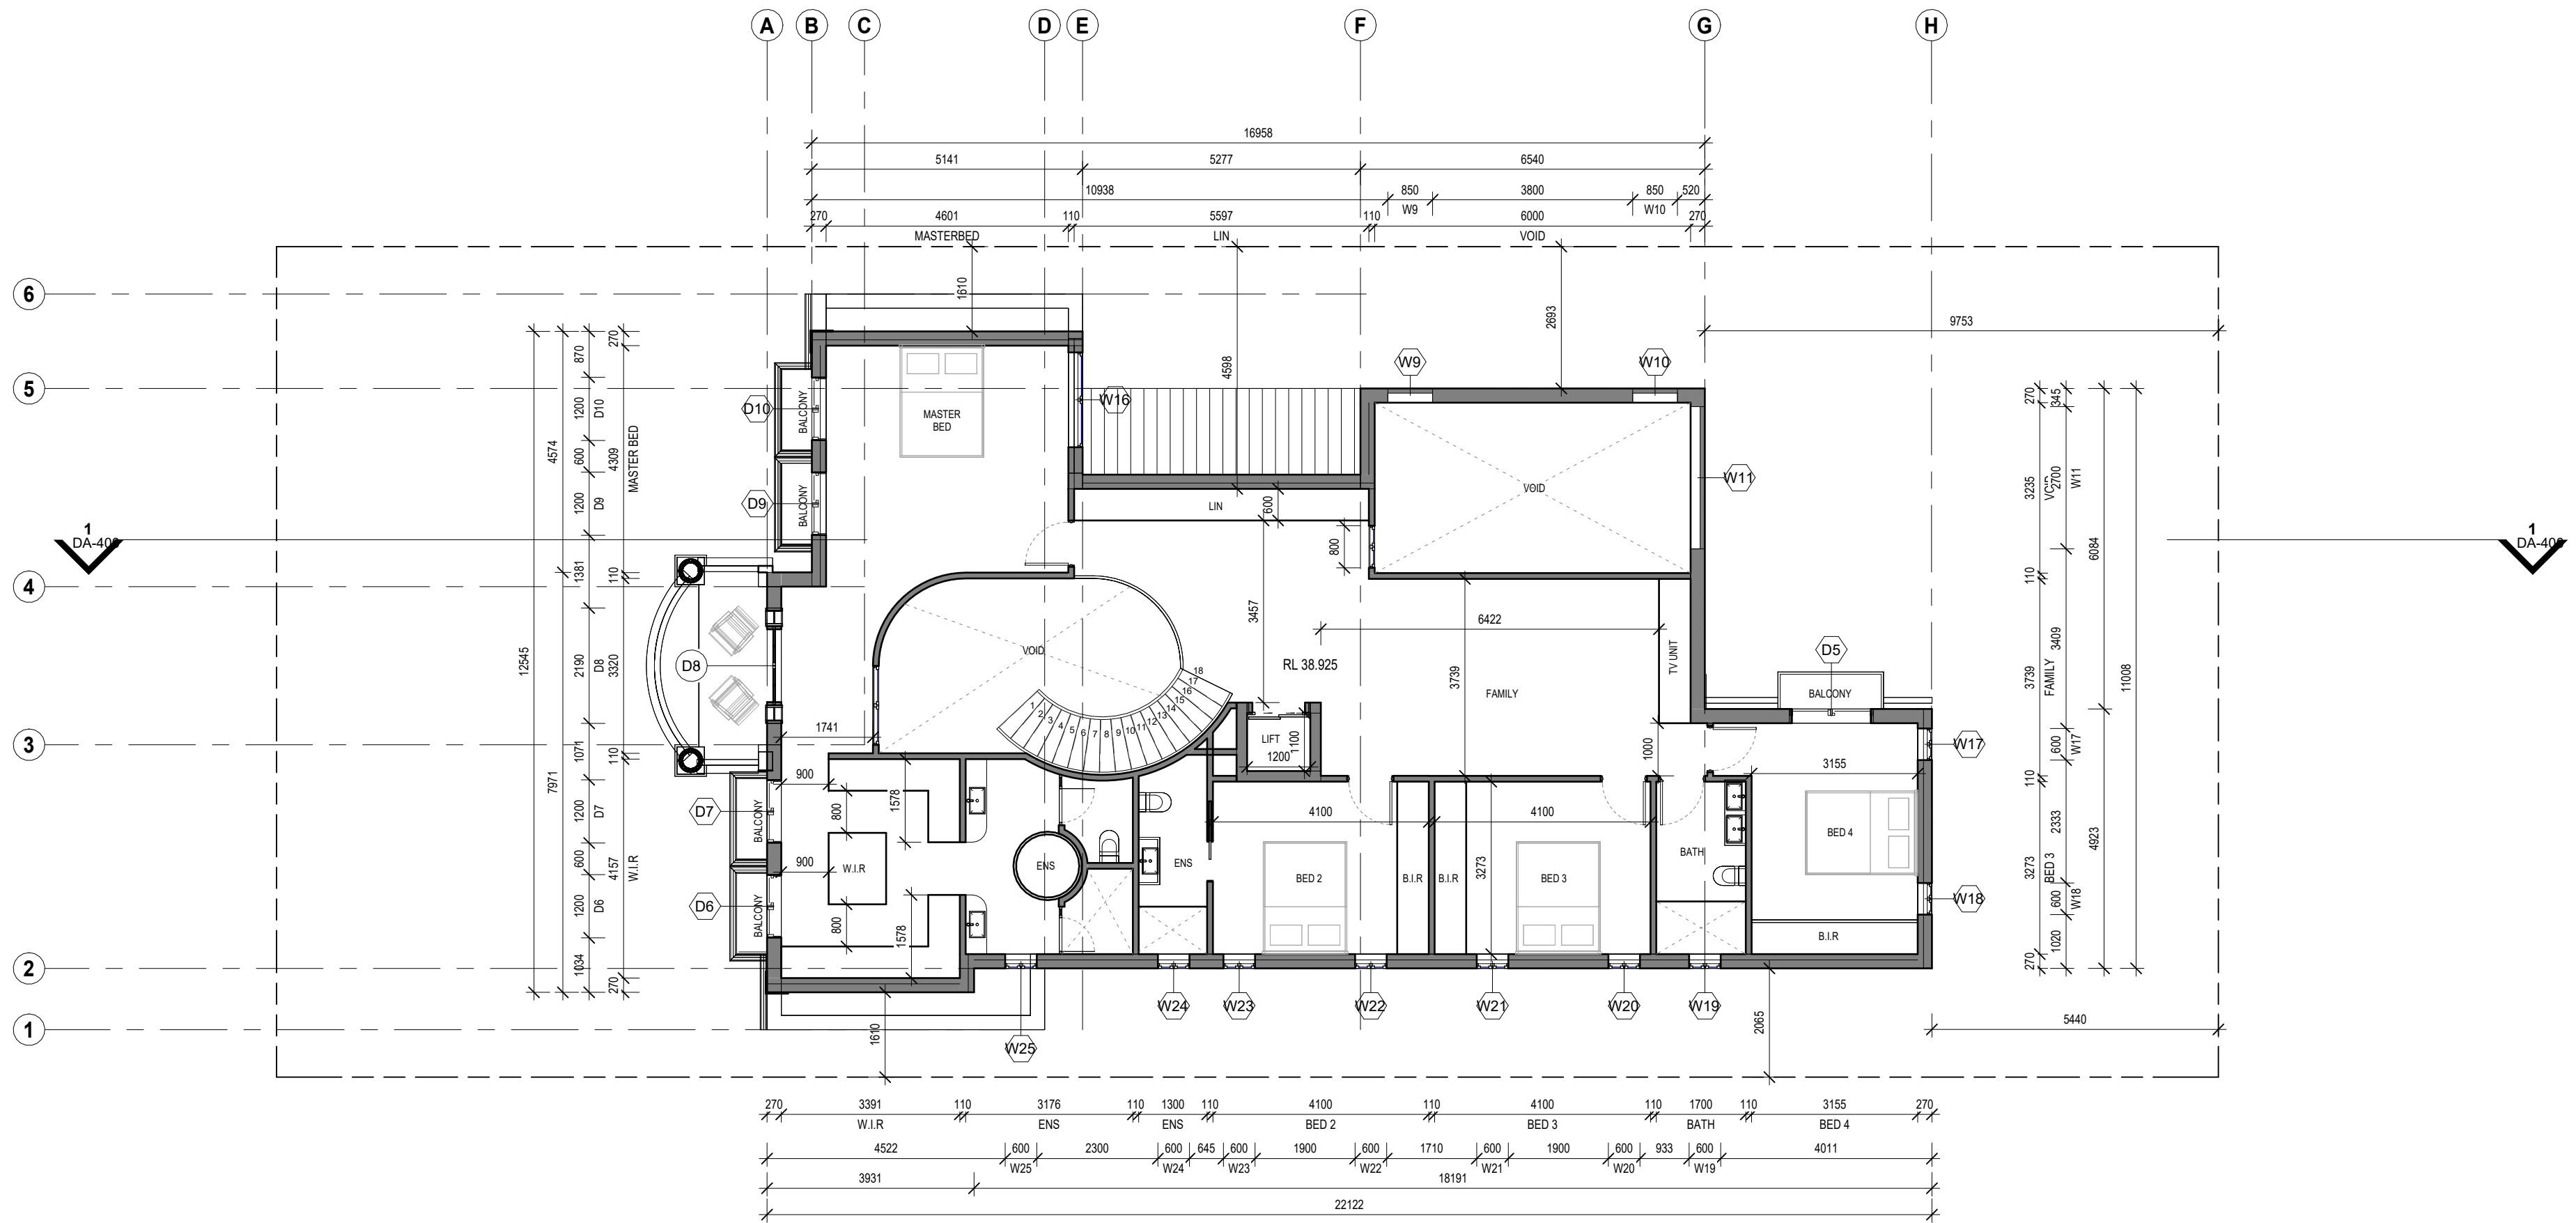


1 05 FIRST FLOOR
1 : 100

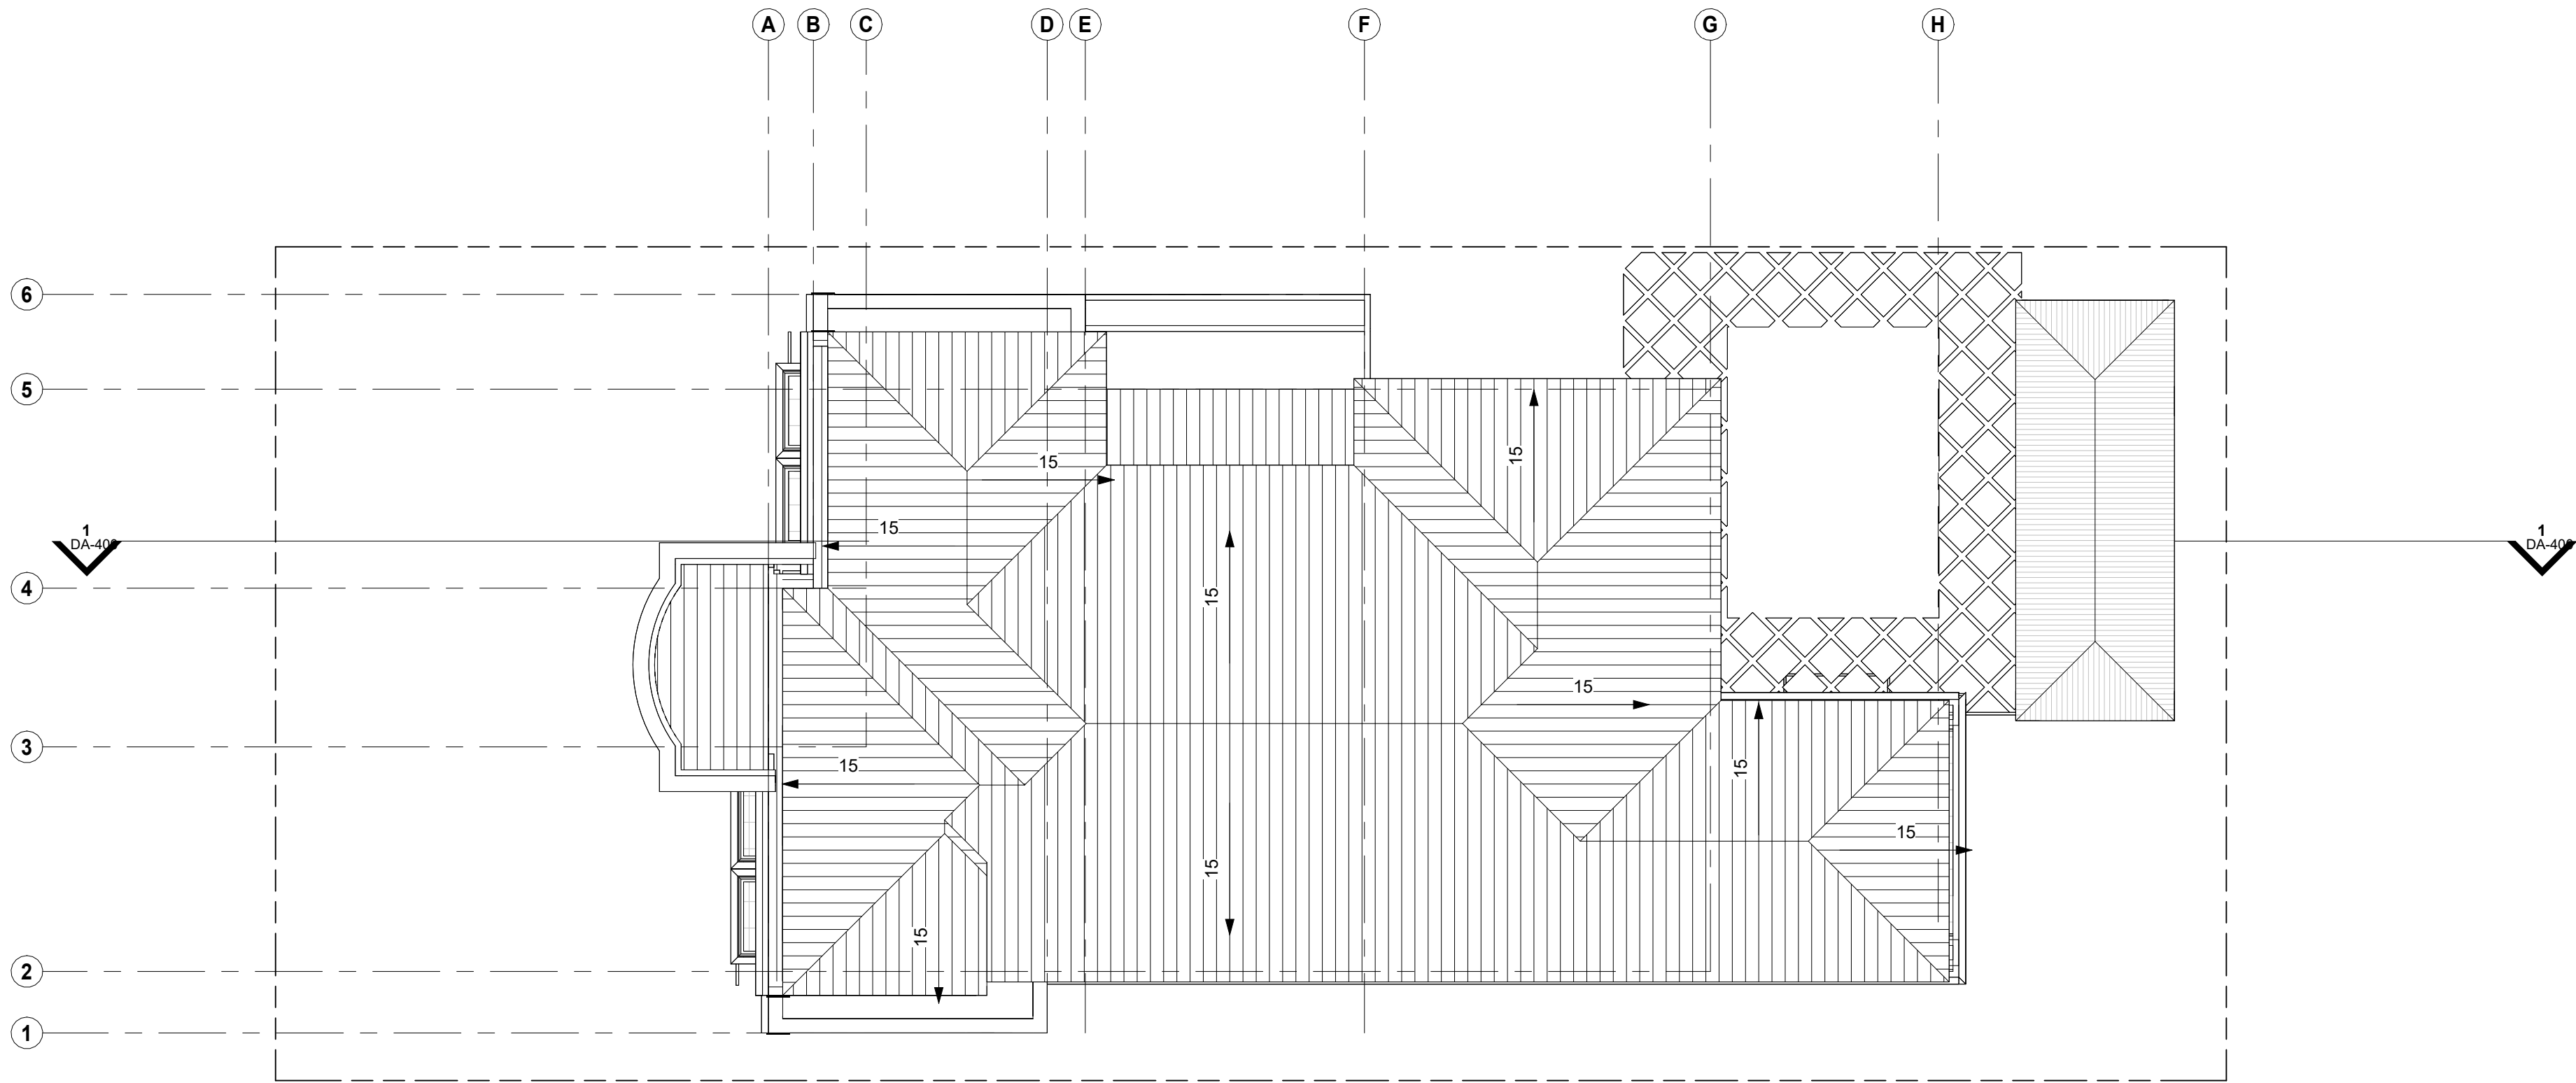


1 ROOF PLAN
1 : 100

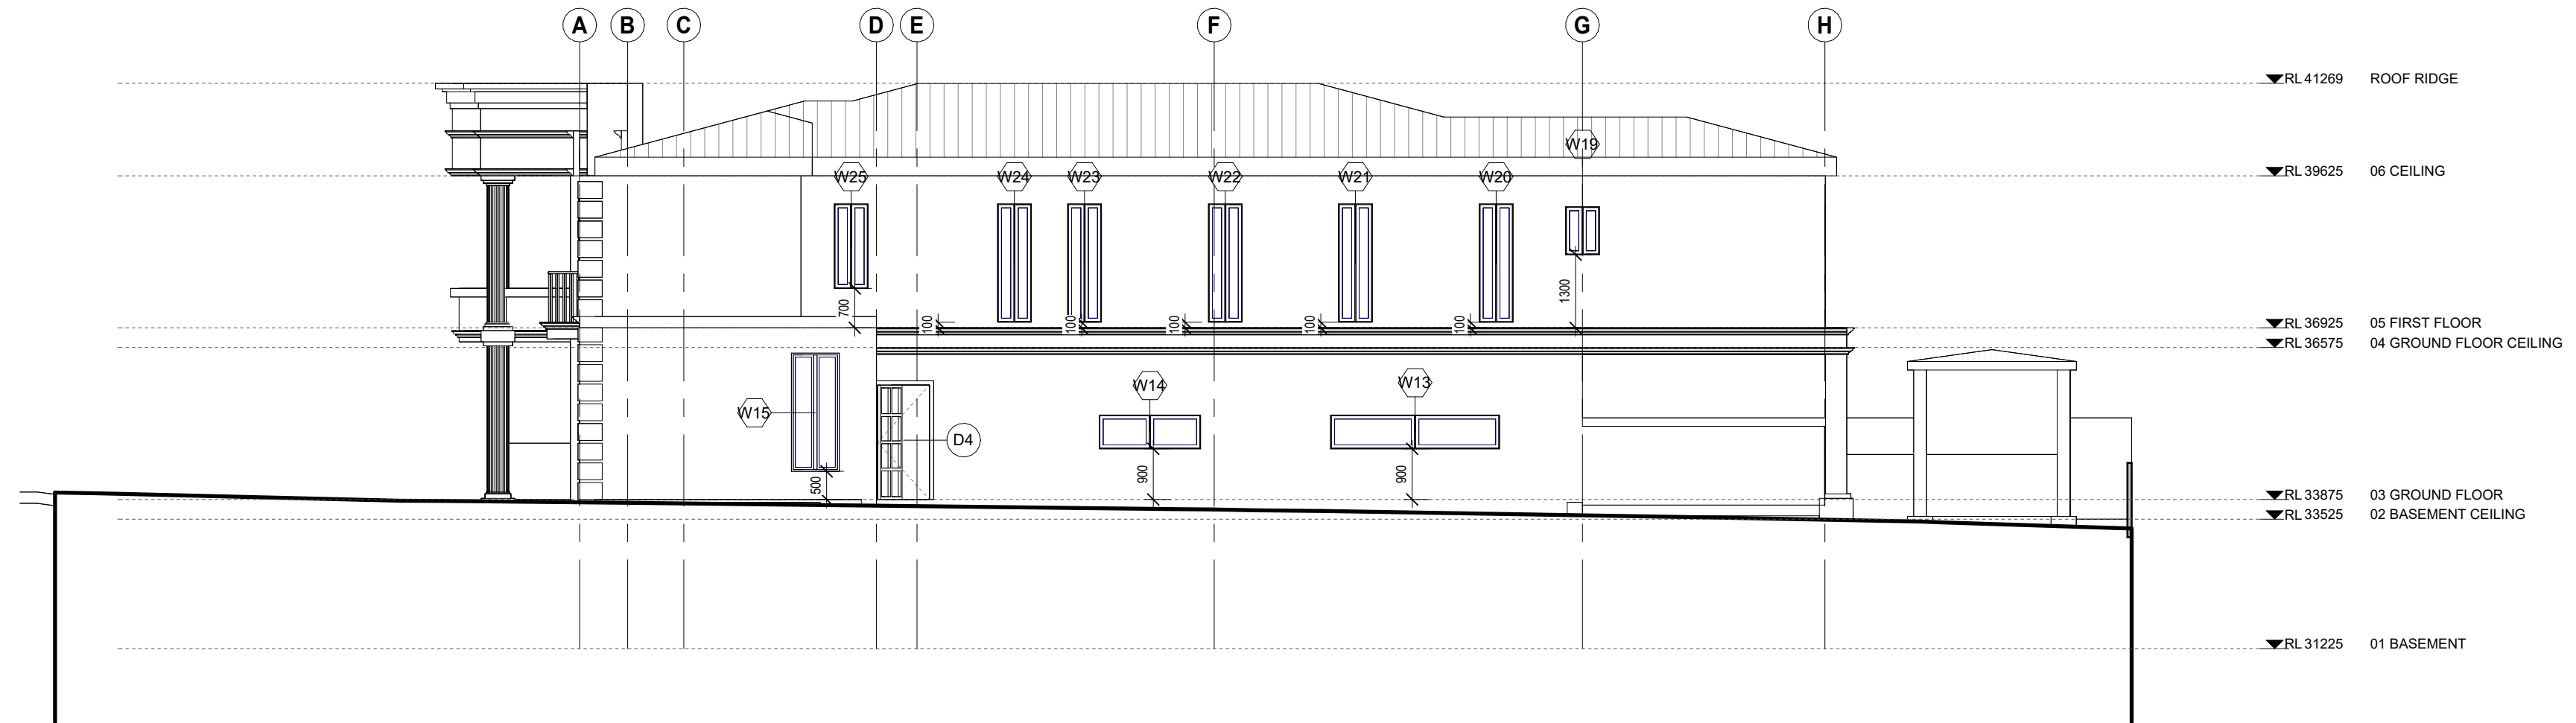

1 SOUTH ELEVATION
1 : 100

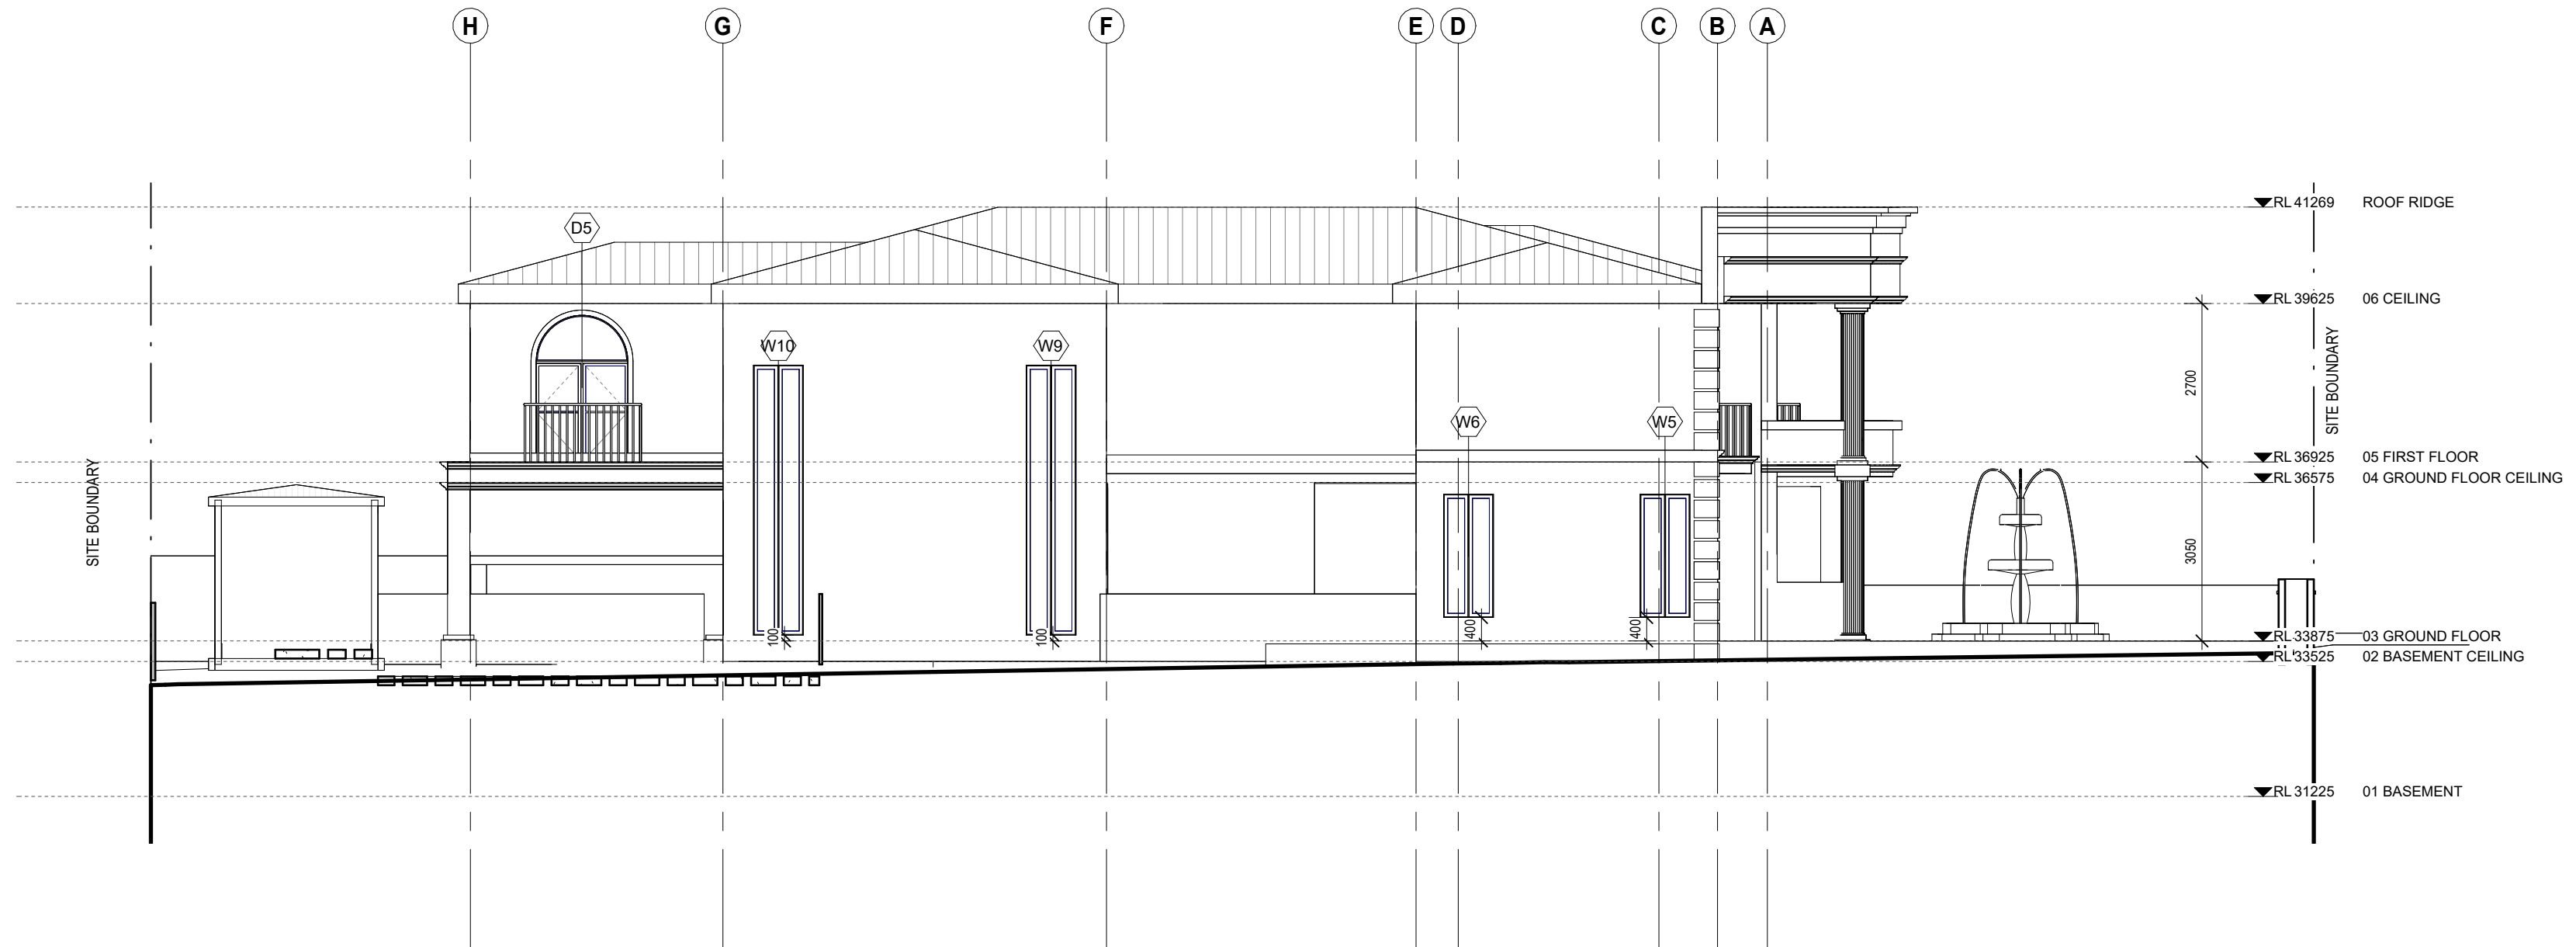


2 NORTH ELEVATION
1 : 100

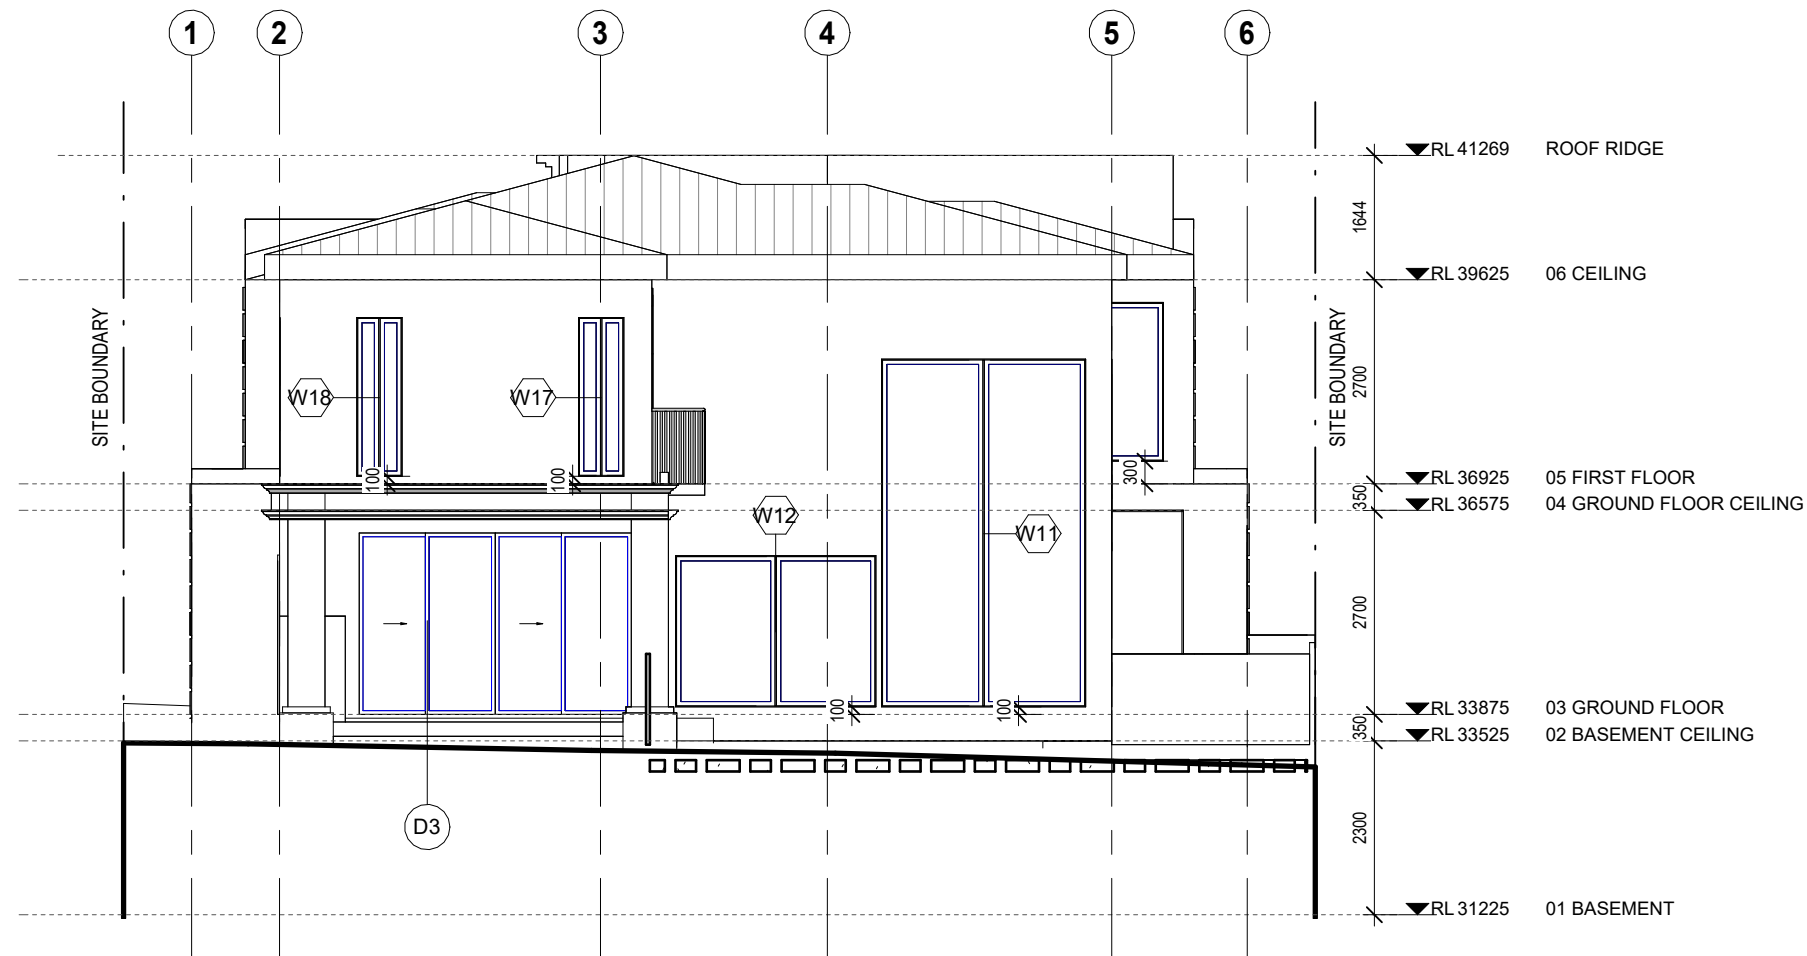


1 EAST ELEVATION
1 : 100




2 WEST ELEVATION
1 : 100

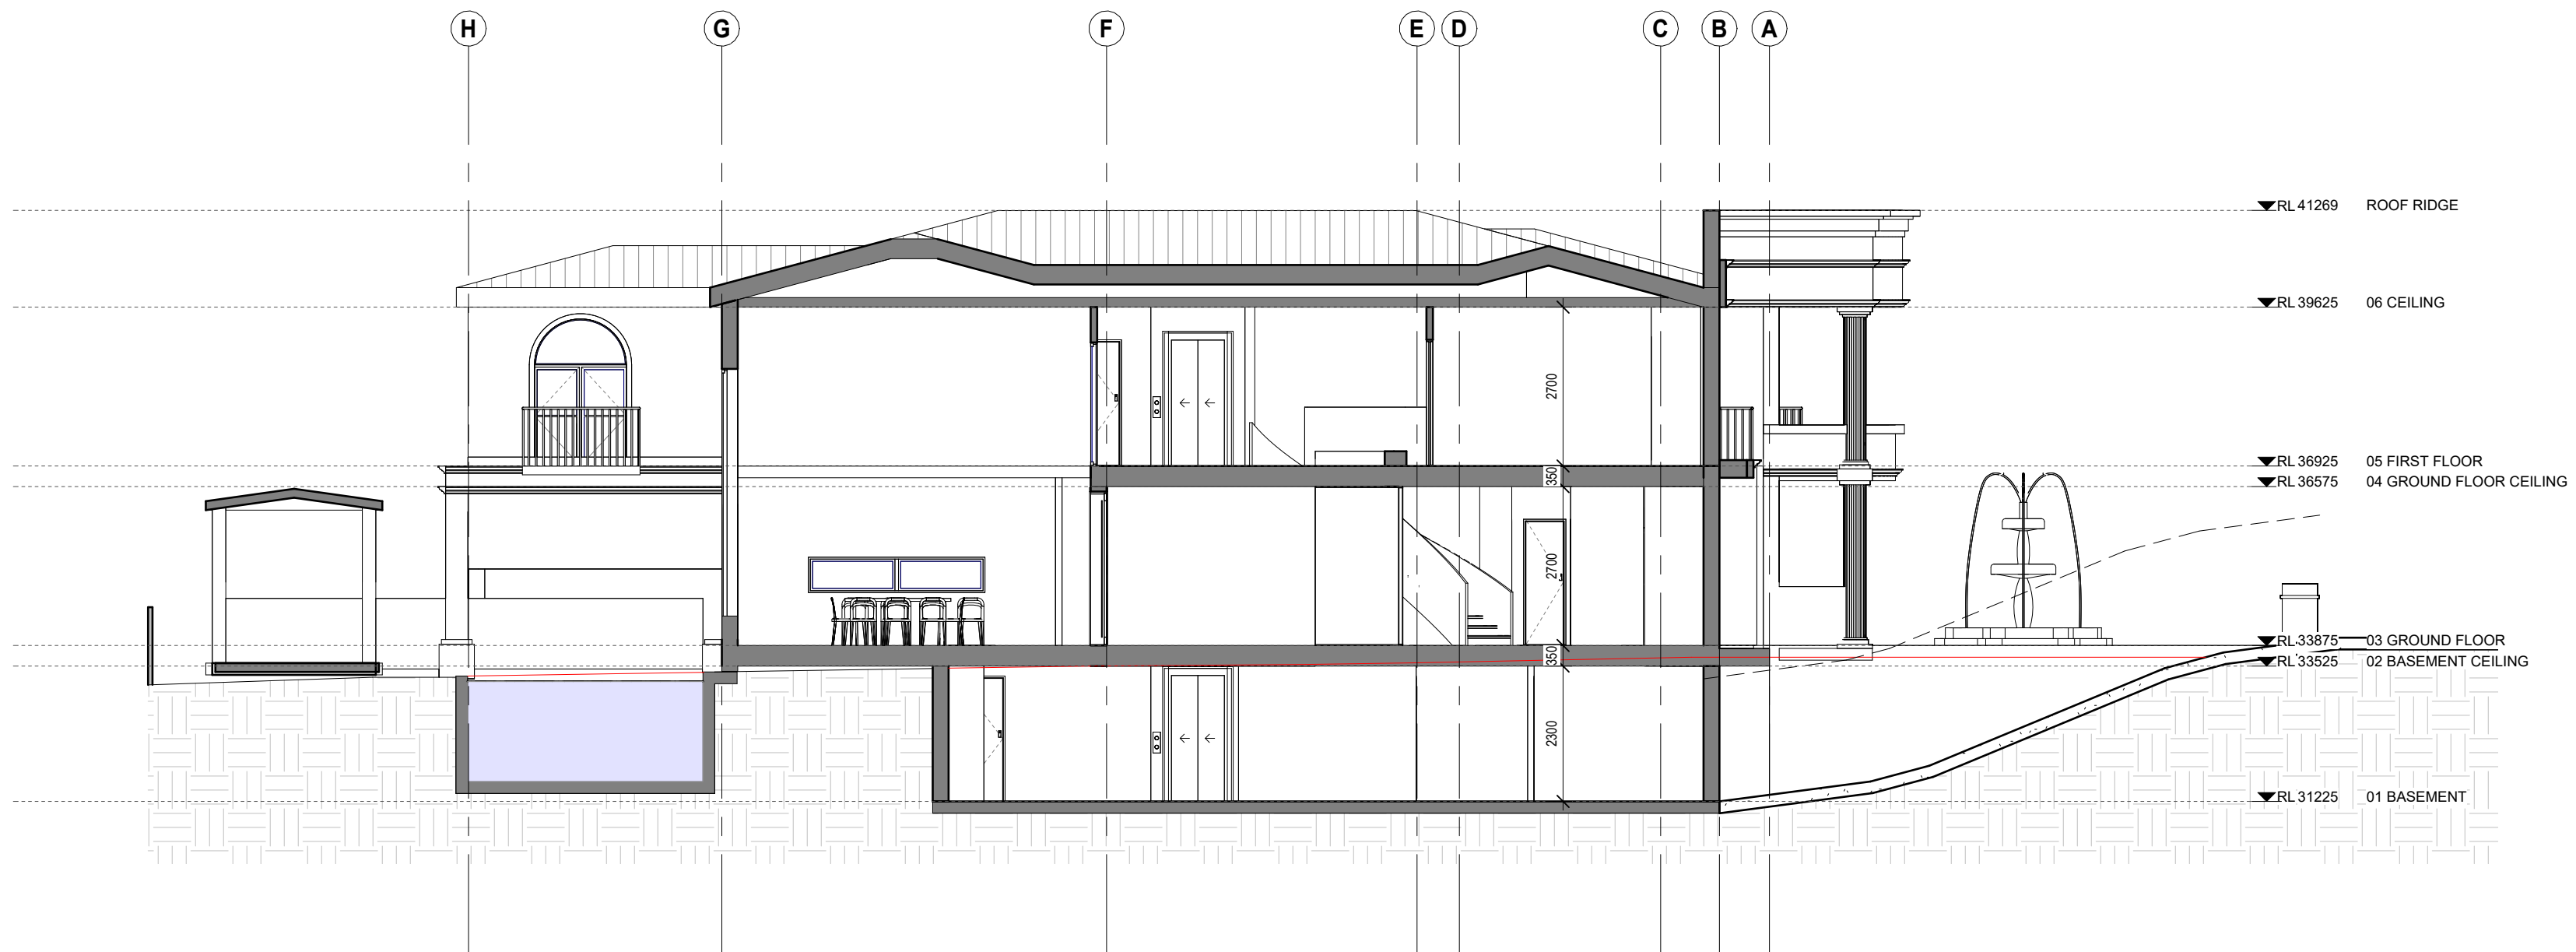


1 SECTION
1 : 100

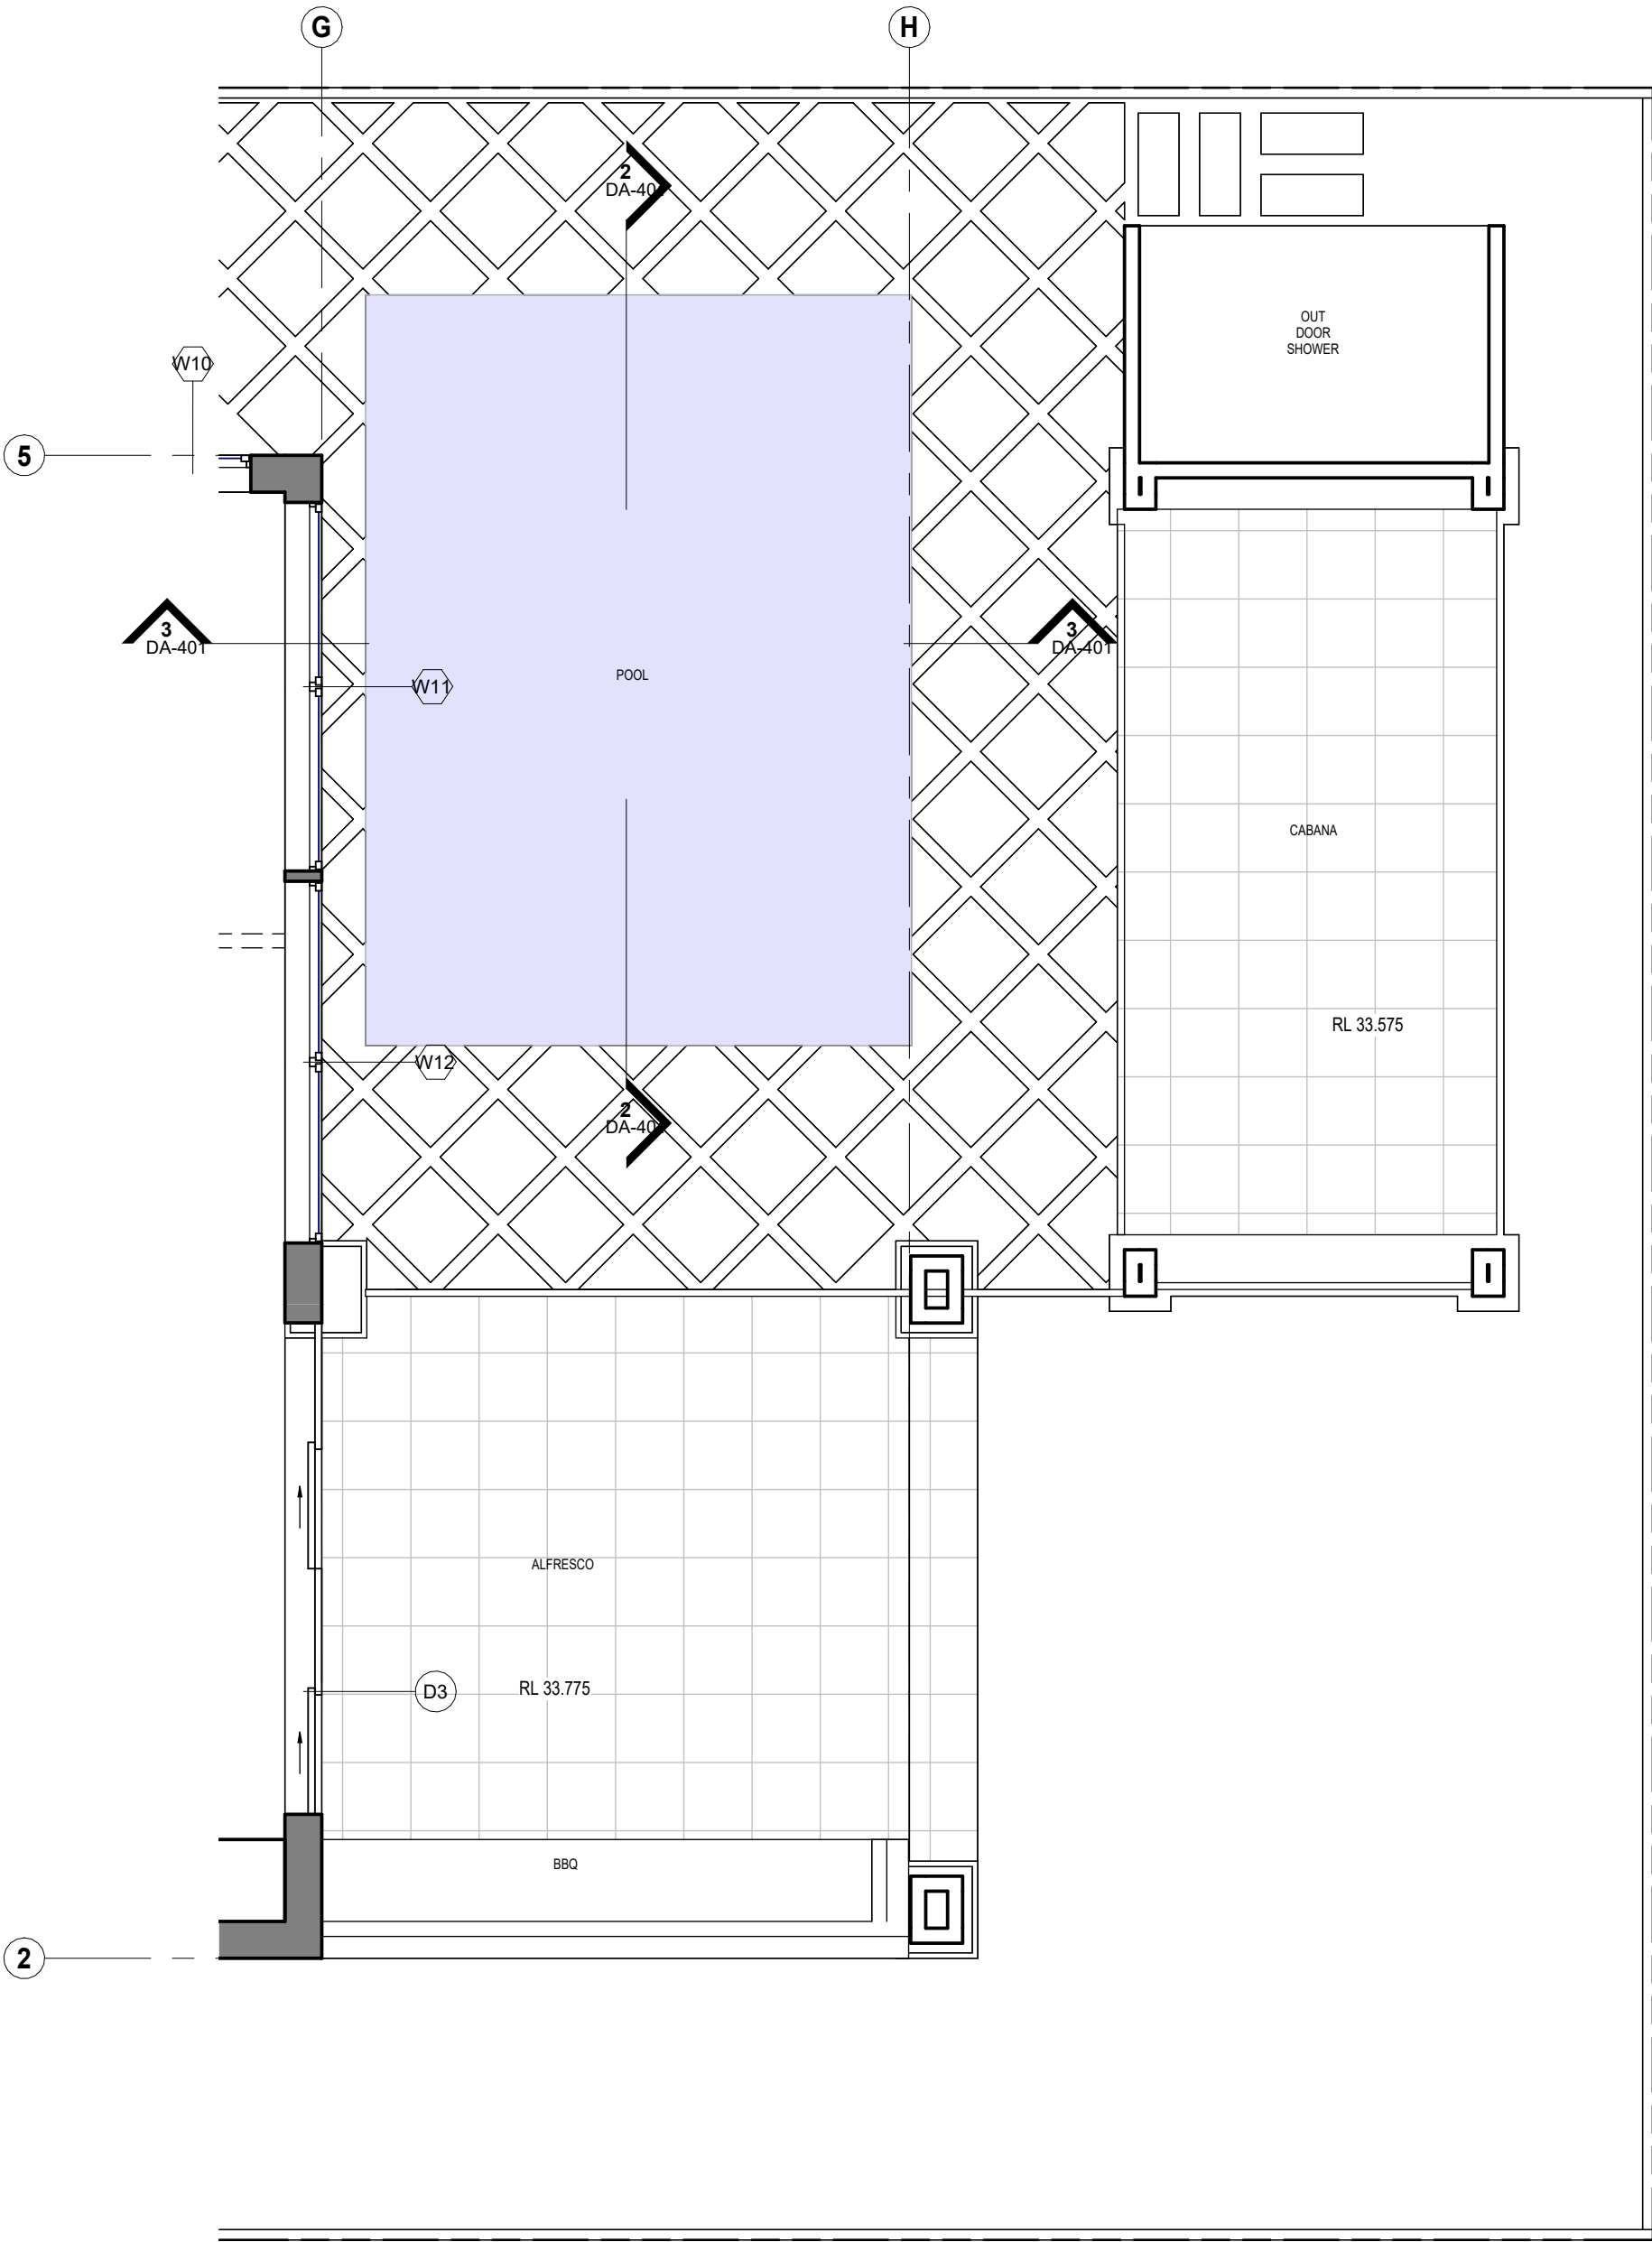


1 POOL
1 : 50

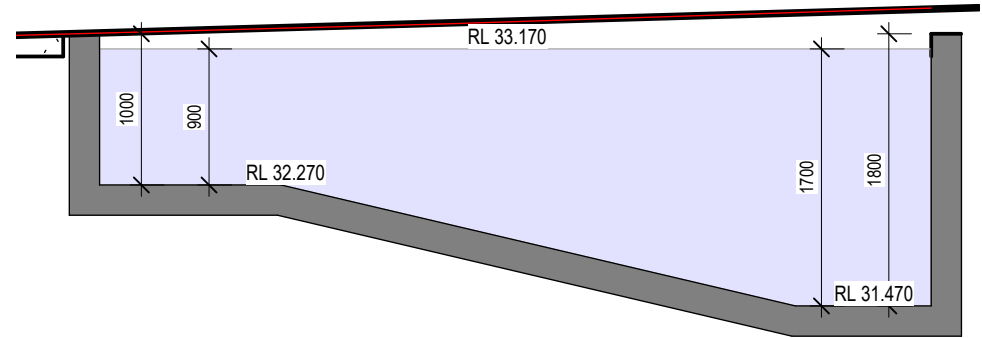


2 POOL LONG SECTION
1 : 50

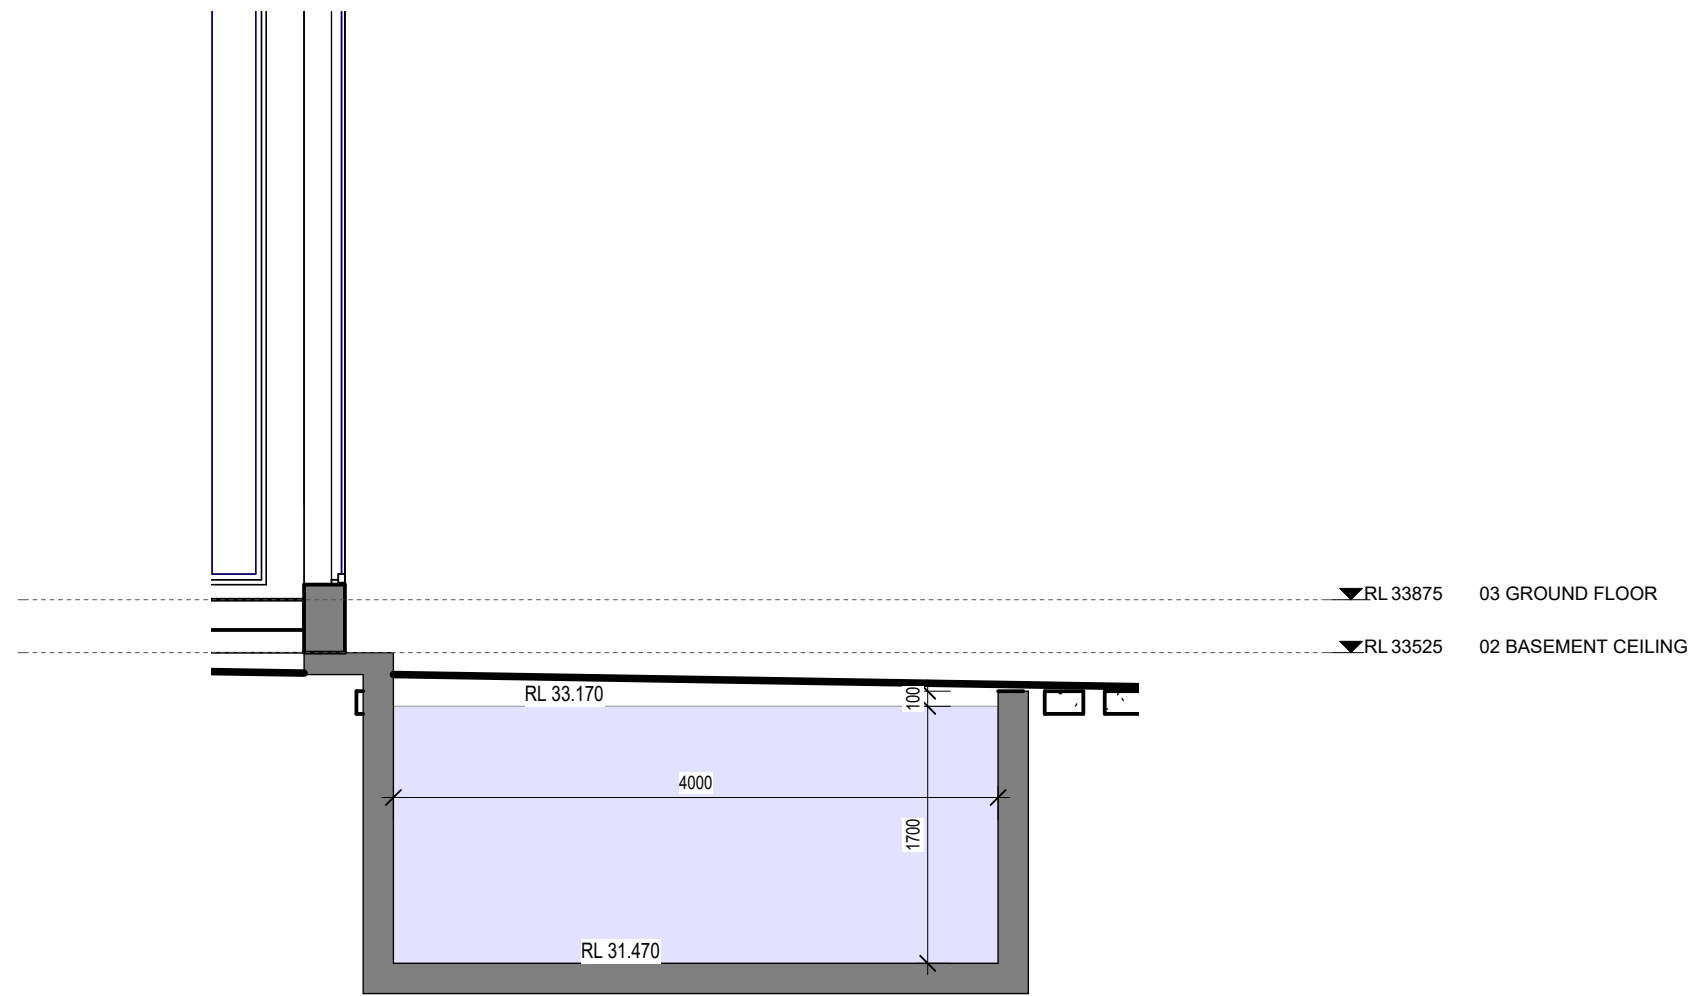


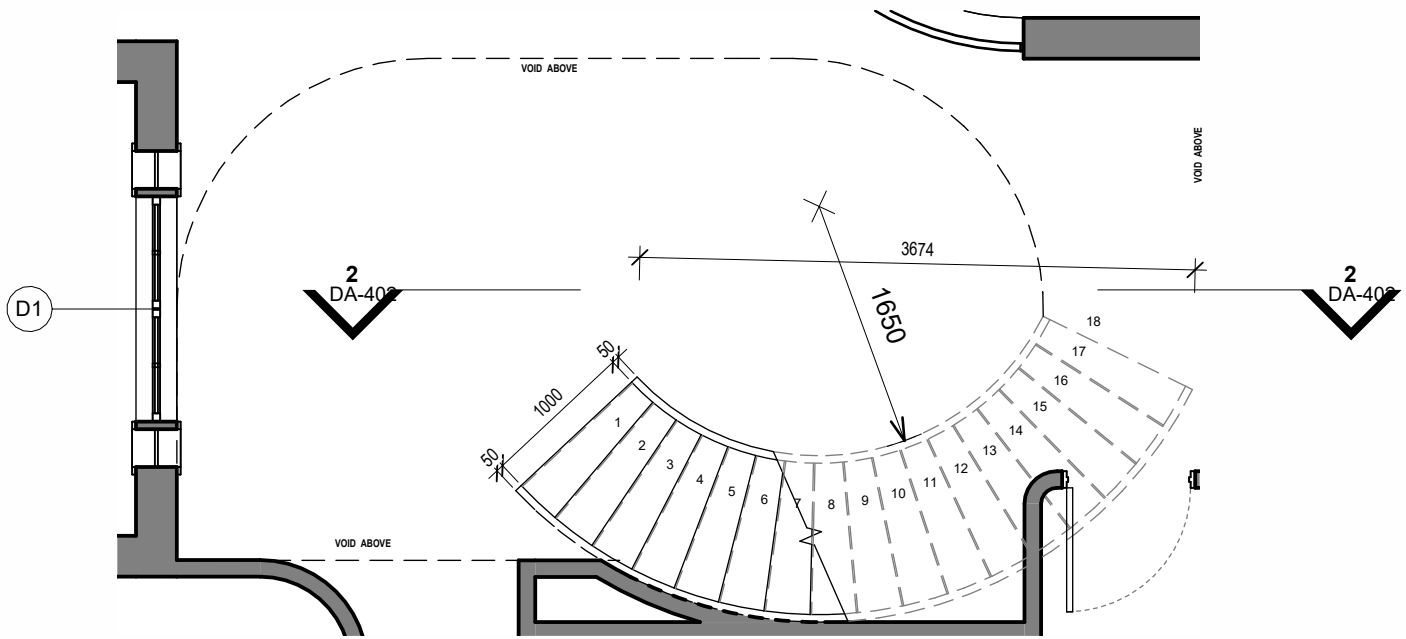


1 GROUND FLOOR STAIRS
1 : 50

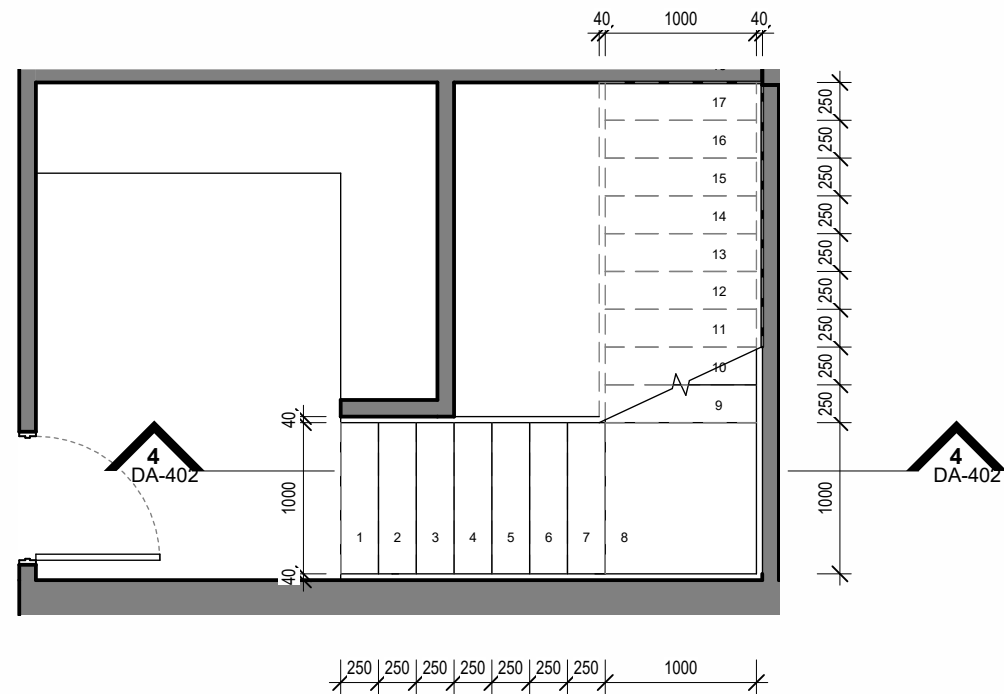


3 BASEMENT STAIRS
1 : 50

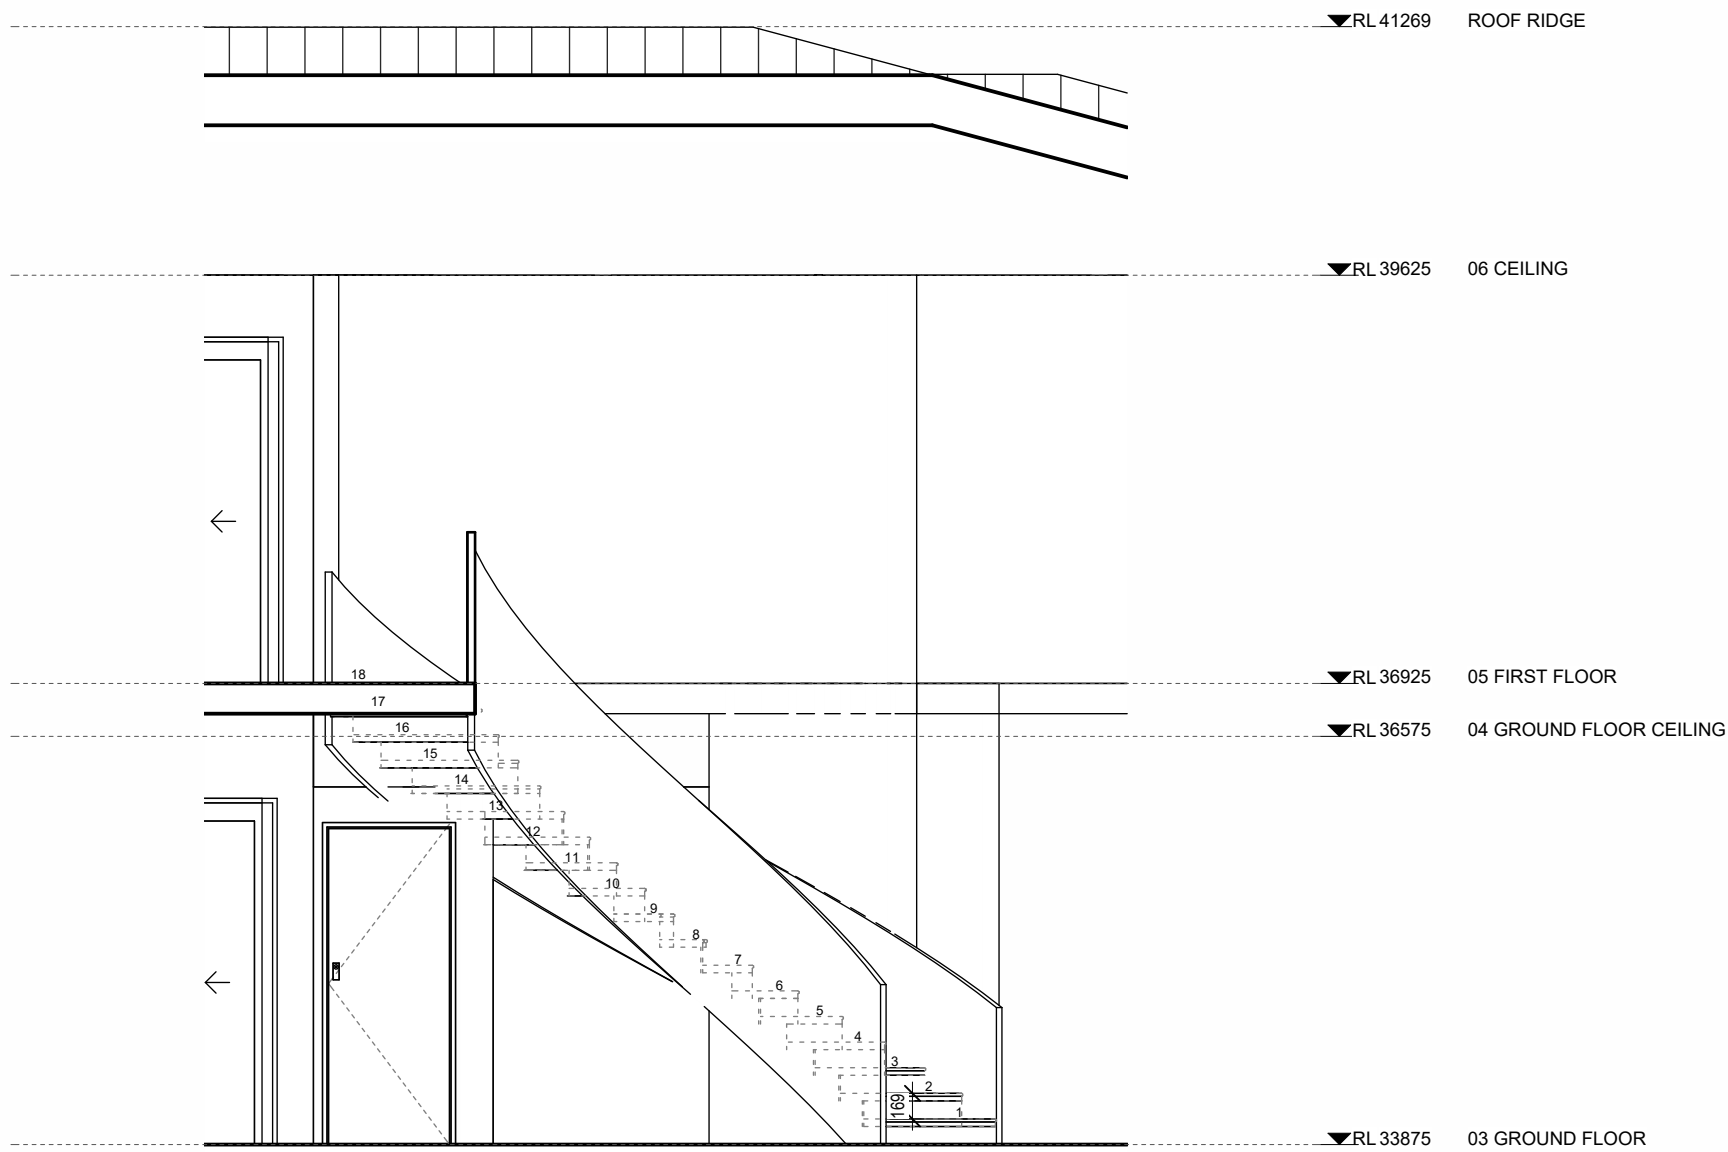

2 GROUND FLOOR STAIR SECTION
1 : 50

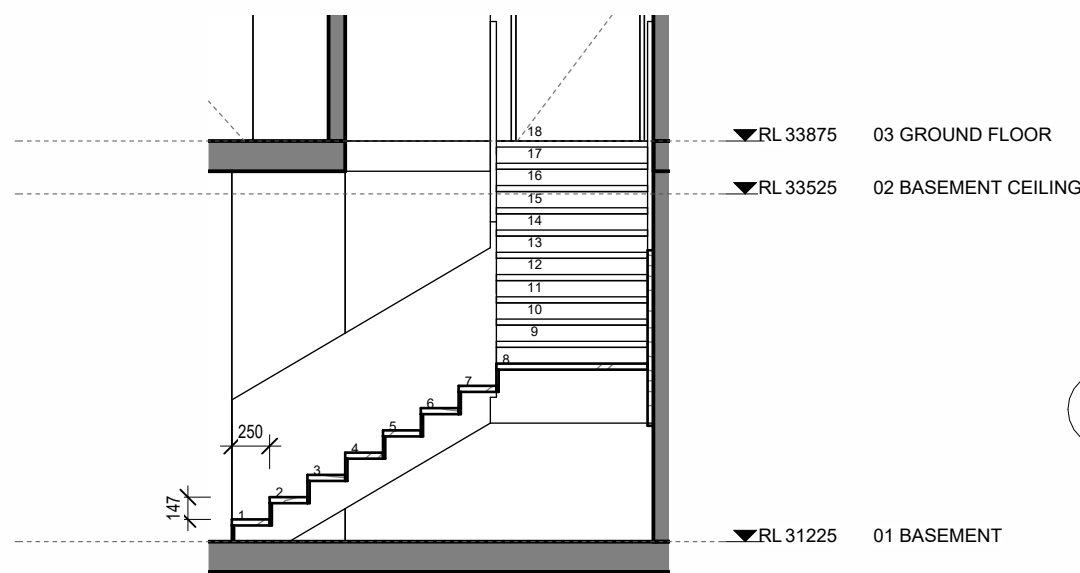

4 BASEMENT STAIR SECTION
1 : 50

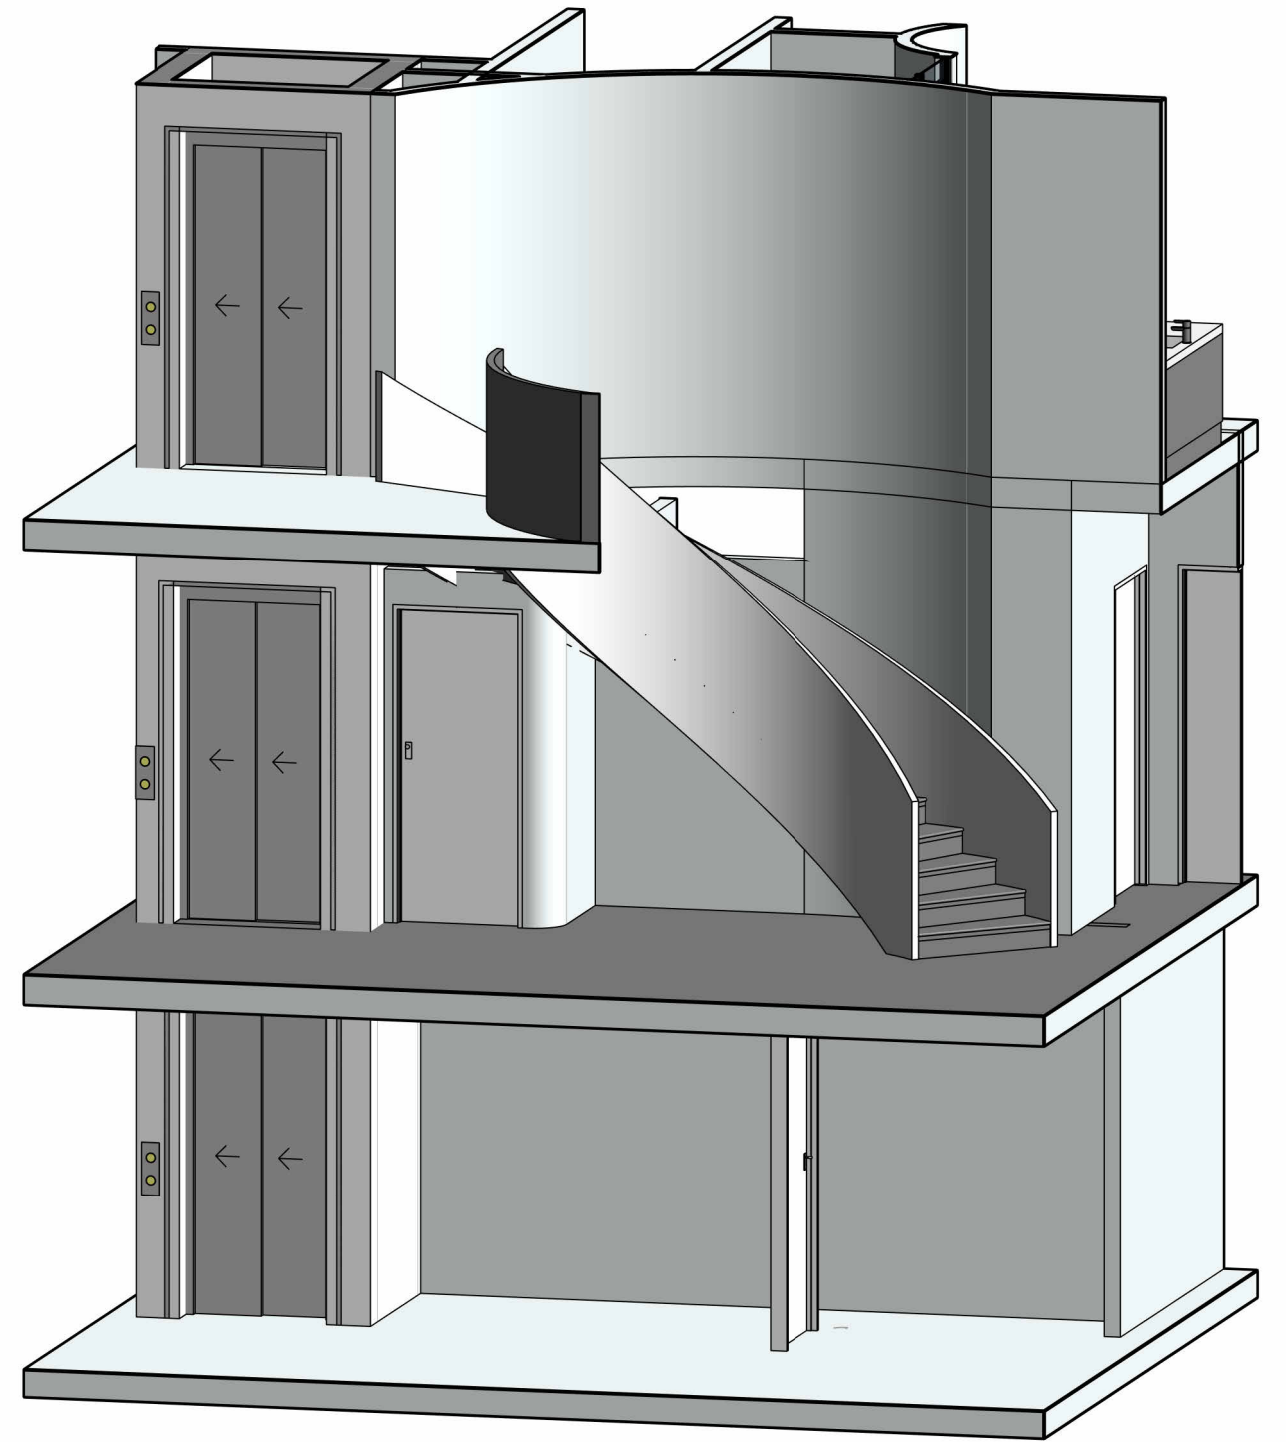

5 STAIR 3D