

LOT 21 IN DP 30370

PROPOSED SECONDARY DWELLING

AT: NO. 5 JOSEPH STREET, BLACKTOWN, NSW 2148



(3D VIEW FOR ILLUSTRATION ONLY)

© THIS DRAWING IS THE PROPERTY OF LT DESIGN & CONSULTING PTY LTD AND WE RESERVE THE COPYRIGHT TO ALL OUR DESIGNS WHICH CANNOT BE REPRODUCED (IN PART OR IN WHOLE) BEFORE FIRST OBTAINING WRITTEN CONSENT. CONTRAVENTION WILL BE PROSECUTED

- FIGURED DIMENSIONS TO BE TAKEN IN PREFERENCE TO SCALE.
- BUILDERS' WORK TO COMPLY WITH THE LATEST BCA AND ITS AMENDMENTS AND RELEVANT AUSTRALIAN STANDARDS REFERRED WITHIN.

No.	Description	Date



DESIGN



BUILDING DESIGNERS AUSTRALIA

Accreditation No: 6302
Shop 6A/80 Thorne Rd, Fairfield West
0414 891 998 - Le@LTDesign.net.au

Building Design | 3D Modeling | Drafting | Detailing

DRAWING:
3D VIEW

CLIENT & PROJECT: LOT 21 IN DP 30370
PROPOSED SECONDARY DWELLING
AT: NO. 5 JOSEPH STREET, BLACKTOWN, NSW 2148

COMPLYING DEVELOPMENT CERTIFICATE

DATE:
15/04/2026

DWG NO:
GF-0626-00

SCALE:



DRW BY:
LT


(A3)

5. SA: SMOKE ALARM
SMOKE ALARMS TO BE INSTALLED IN ACCORDANCE
WITH AS 3786-2014 & CONNECTED TO MAINS POWER

SITE AREA: 581.7 SQM	EXISTING	PROPOSED	REQUIRED	COMPLY
EXISTING GROUND FLOOR	114.5 sqm			
EXISTING FIRST FLOOR	55.3 sqm			
EXISTING GARAGE	31.5 sqm		EXCLUDED 18 sqm	
PROPOSED 2ND DWELLING		60 sqm	60 sqm (Max.)	YES
TOTAL FLOOR AREA	243.3 sqm		330 sqm (Max.)	YES
PRIVATE OPEN SPACE	24.1 sqm		> 24 sqm	YES
LANDSCAPE AREA	(198.7 sqm) 34.1%		20% (Min.)	YES
SITE COVERAGE	(206.0 sqm) 35.4%		50% (Max.)	YES

ITEM	HEIGHT	WIDTH	ORIENTATION
W1	1200	1500	
W2	900	400	
W3	400	1200	
W4	1200	1500	
W5	1200	1500	
W6	900	1000	

1 : 200

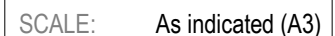[illegible]


- LOH

: LIFT OFF HINGES DOOR TO COMPLY WITH NCC 2022
- SA

: SMOKE ALARM TO COMPLY WITH AS.3786
- FW

: FLOOR WASTE
- MV

: MECHANICAL VENTILATION

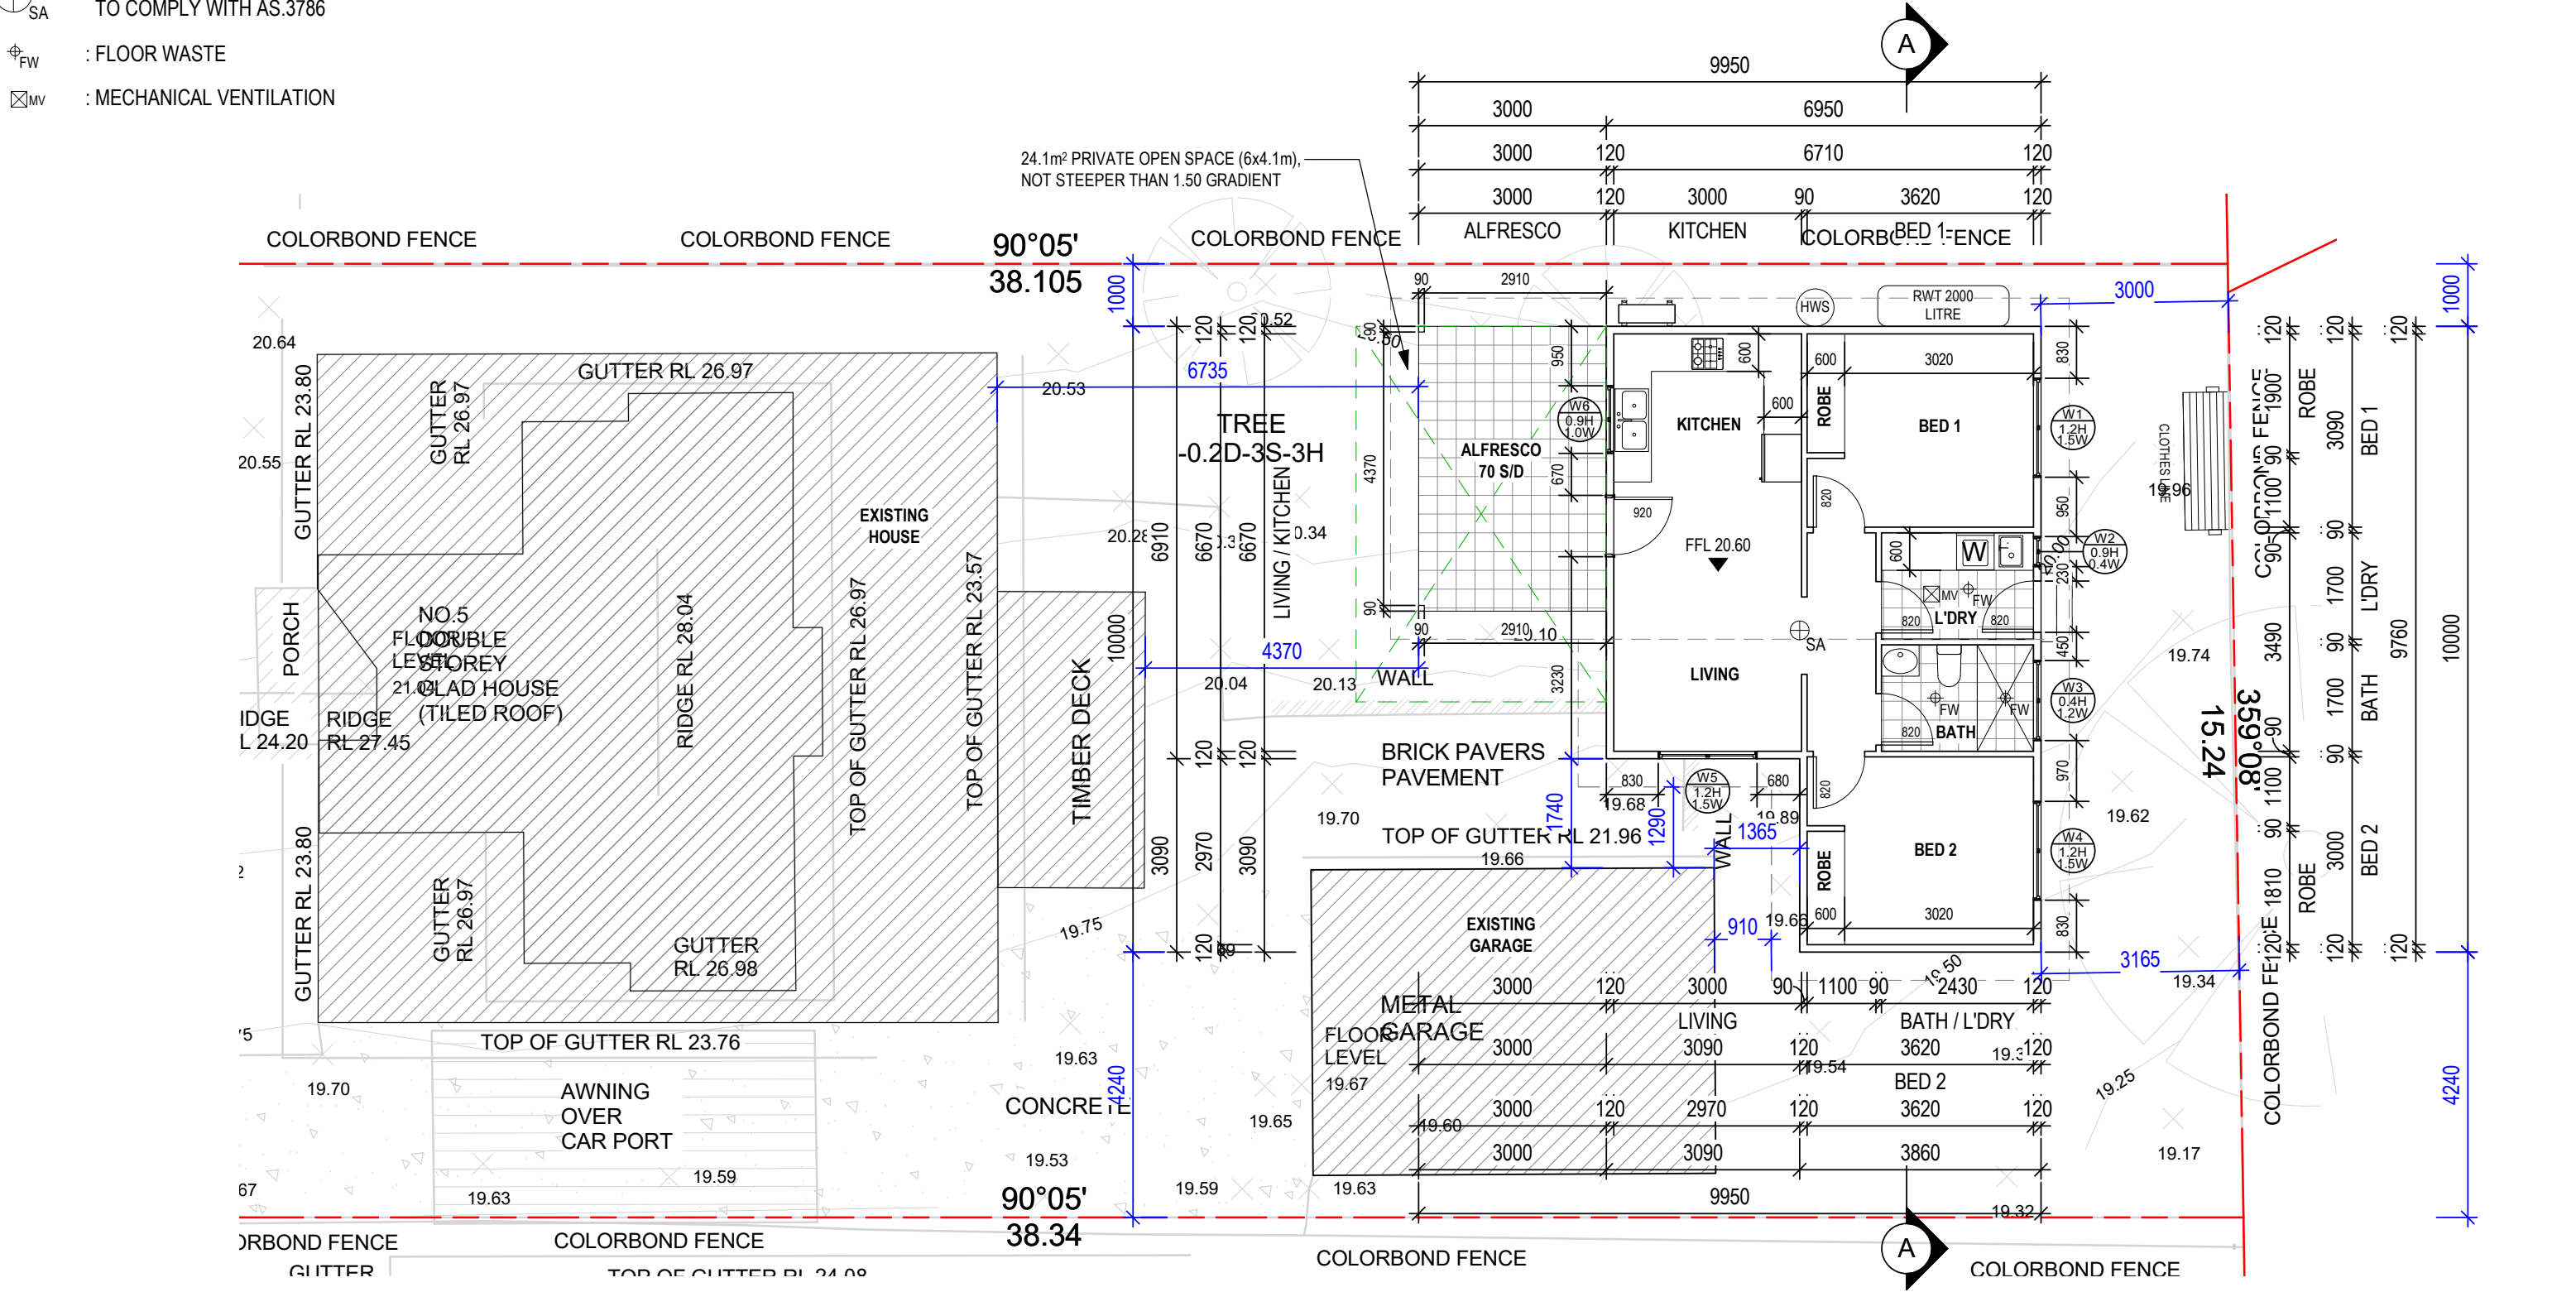

1 PROPOSED GROUND FLOOR PLAN
1 : 100

© THIS DRAWING IS THE PROPERTY OF LT DESIGN & CONSULTING PTY LTD AND WE RESERVE THE COPYRIGHT TO ALL OUR DESIGNS WHICH CANNOT BE REPRODUCED (IN PART OR IN WHOLE) BEFORE FIRST OBTAINING WRITTEN CONSENT. CONTRAVENTION WILL BE PROSECUTED

FIGURED DIMENSIONS TO BE TAKEN IN PREFERENCE TO SCALE.

BUILDERS' WORK TO COMPLY WITH THE LATEST BCA AND ITS AMENDMENTS AND RELEVANT AUSTRALIAN STANDARDS REFERRED WITHIN.

No.	Description	Date

LT

DESIGN

bda

BUILDING DESIGNERS AUSTRALIA

Accreditation No: 6302

Shop 6A/80 Thorney Rd, Fairfield West

0414 891 998 - Le@LTDesign.net.au

Building Design

3D Modeling

Drafting

Detailing

DRAWING:
PROPOSED GROUND FLOOR PLAN

CLIENT & PROJECT: LOT 21 IN DP 30370

PROPOSED SECONDARY DWELLING

AT: NO. 5 JOSEPH STREET, BLACKTOWN, NSW 2148

COMPLYING DEVELOPMENT CERTIFICATE


DATE:
15/04/2026

DWG NO:
GF-0626-02


SCALE:
1 : 100 (A3)

DRW BY:
LT


NOTE:
EAVES ENCROACHING WITHIN 900mm
OF AN ALLOTMENT BOUNDARY AND
1800mm FROM ANOTHER BUILDING
TO BE NON-COMBUSTILE

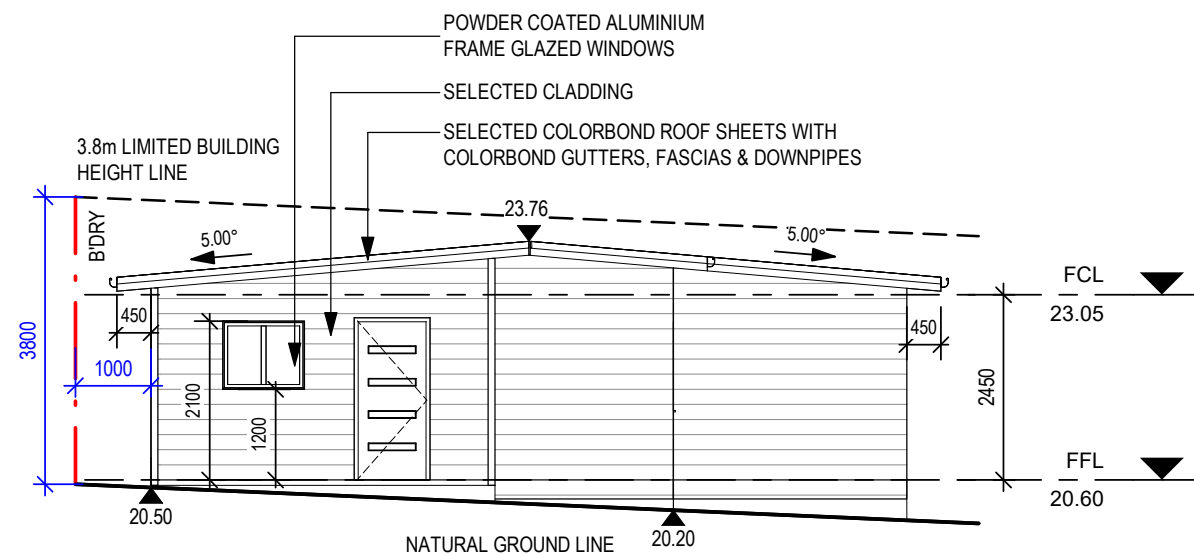


① WEST ELEVATION
1 : 100

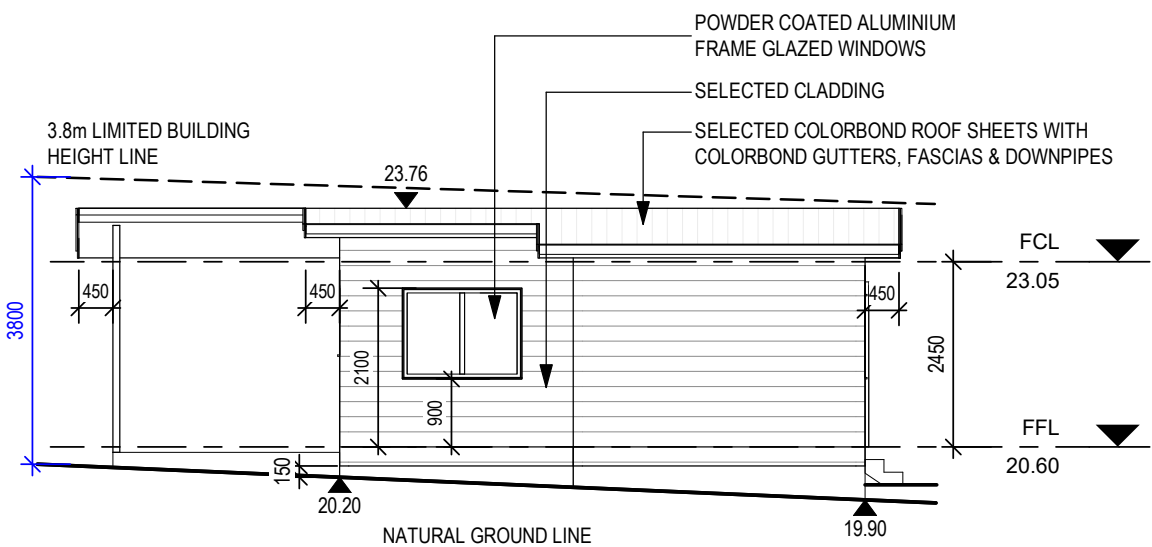

② SOUTH ELEVATION
1 : 100

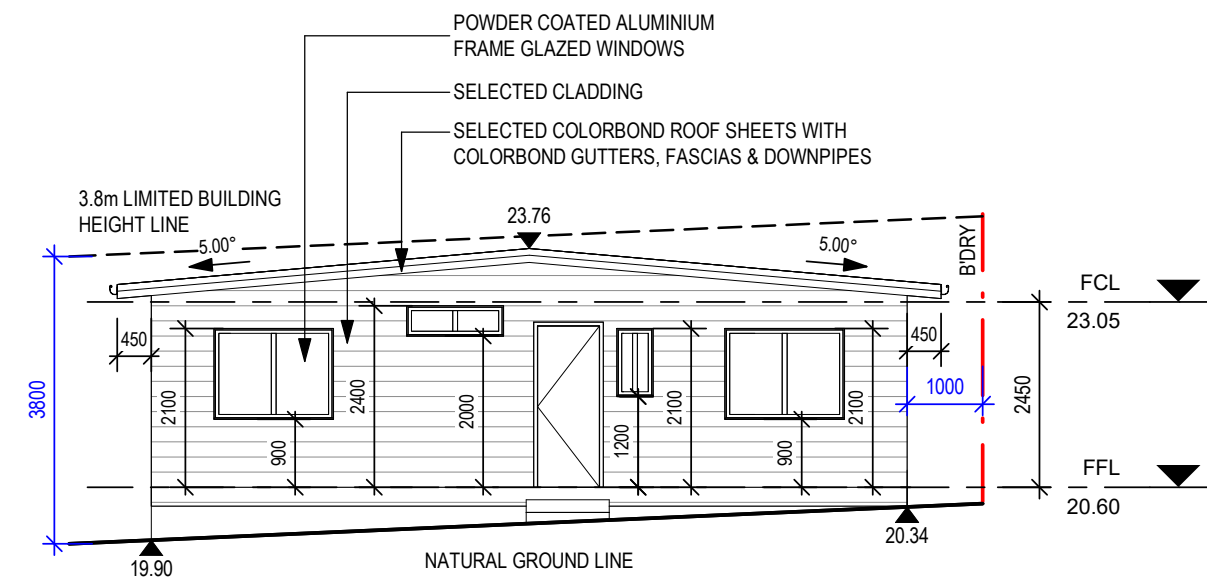

③ EAST ELEVATION
1 : 100

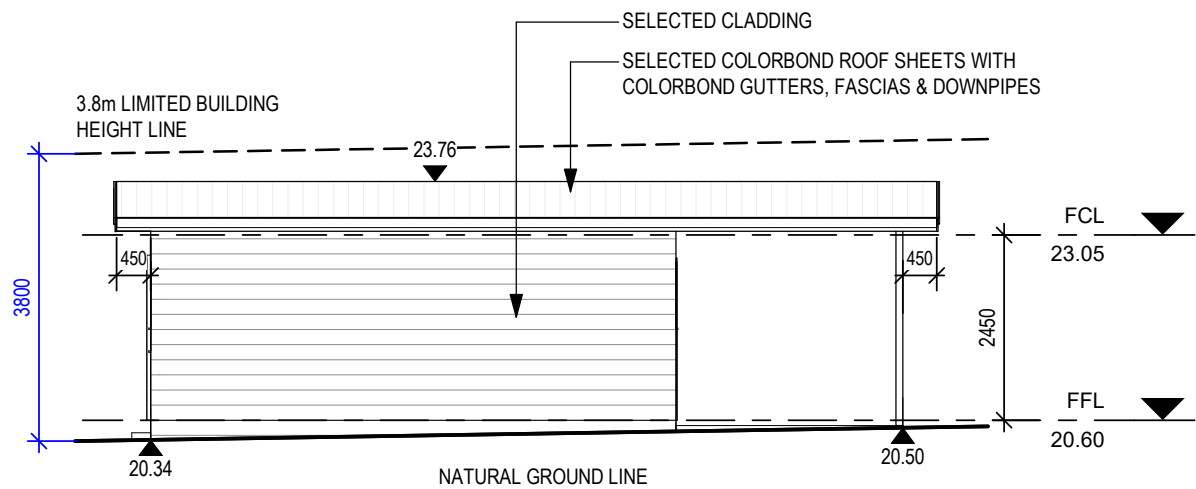

④ NORTH ELEVATION
1 : 100

© THIS DRAWING IS THE PROPERTY OF LT DESIGN & CONSULTING PTY LTD AND WE RESERVE THE COPYRIGHT TO ALL OUR DESIGNS WHICH CANNOT BE REPRODUCED (IN PART OR IN WHOLE) BEFORE FIRST OBTAINING WRITTEN CONSENT. CONTRAVENTION WILL BE PROSECUTED

- FIGURED DIMENSIONS TO BE TAKEN IN PREFERENCE TO SCALE.
- BUILDERS' WORK TO COMPLY WITH THE LATEST BCA AND ITS AMENDMENTS AND RELEVANT AUSTRALIAN STANDARDS REFERRED WITHIN.

No.	Description	Date



Building Design | 3D Modeling | Drafting | Detailing



Accreditation No: 6302
Shop 6A/80 Thorney Rd, Fairfield West
0414 891 998 - Le@LTDesign.net.au

DRAWING:
ELEVATIONS

CLIENT & PROJECT: LOT 21 IN DP 30370
PROPOSED SECONDARY DWELLING
AT: NO. 5 JOSEPH STREET, BLACKTOWN, NSW 2148

COMPLYING DEVELOPMENT CERTIFICATE

DATE:
15/04/2026
DWG NO:
GF-0626-03




DRW BY:
LT

SCALE: 1 : 100 (A3)


Condensation Management Details

- (1) An exhaust system installed in a kitchen, bathroom, sanitary compartment or laundry must have a minimum flow rate of—
- (a)25 L/s for a bathroom or sanitary compartment; and
 - (b)40 L/s for a kitchen or laundry.
- (2) Exhaust from a kitchen, kitchen range hood, bathroom, sanitary compartment or laundry must discharge directly or via a shaft or duct to outdoor air.
- (3) Where a venting clothes dryer is installed, it must discharge directly or via a shaft or duct to outdoor air.
- (4) An exhaust system that is not run continuously and is serving a bathroom or sanitary compartment that is not ventilated in accordance with 10.6.2(a) must—
- (a)be interlocked with the room’s light switch; and
 - (b)include a run-on timer so that the exhaust system continues to operate for 10 minutes after the light switch is turned off.
- (5) Except for rooms that are ventilated in accordance with 10.6.2(a), a room with an exhaust system in accordance with (1) must be provided with make-up air—
- (a)via openings to an adjacent room with a free area of 14,000 mm2; or in accordance with AS 1668.2.

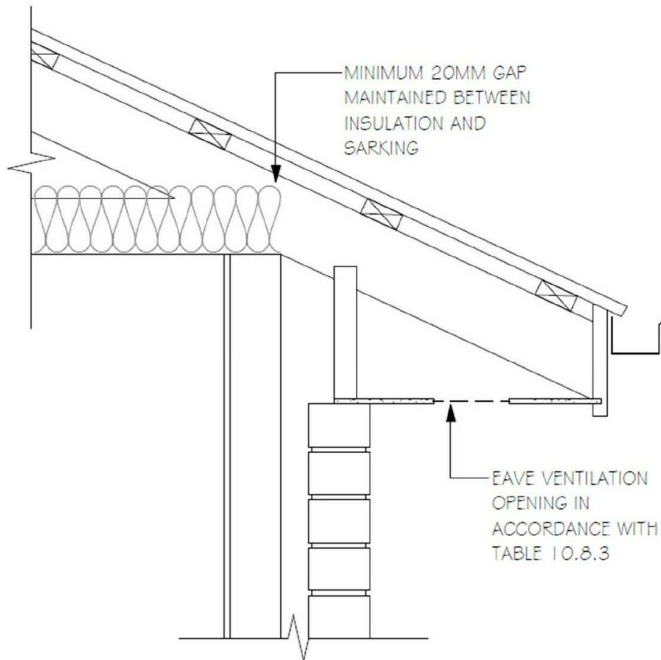

CONDENSATION MANAGEMENT DETAILS

NOTE:
EAVES ENCROACHING WITHIN 900mm OF AN ALLOTMENT BOUNDARY AND 1800mm FROM ANOTHER BUILDING TO BE NON-COMBUSTILE

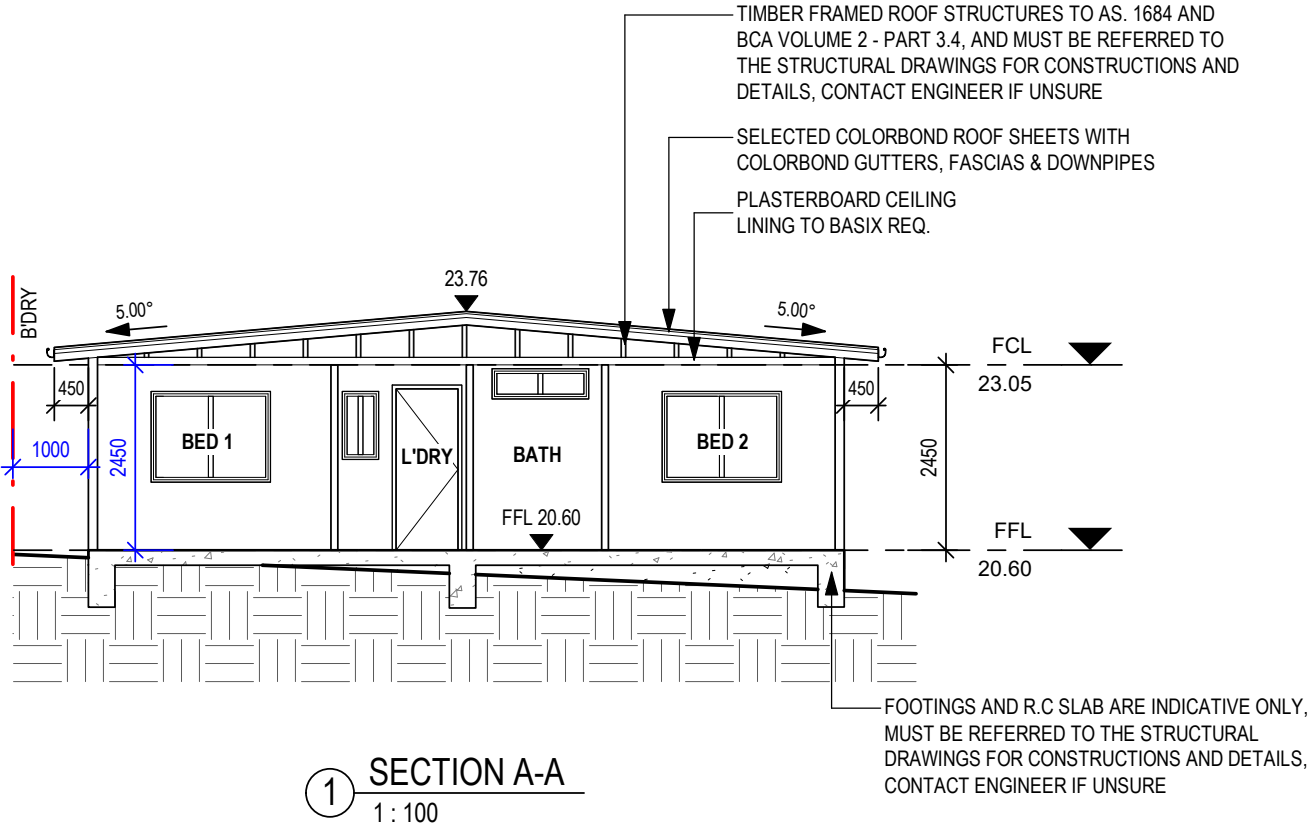

© THIS DRAWING IS THE PROPERTY OF LT DESIGN & CONSULTING PTY LTD AND WE RESERVE THE COPYRIGHT TO ALL OUR DESIGNS WHICH CANNOT BE REPRODUCED (IN PART OR IN WHOLE) BEFORE FIRST OBTAINING WRITTEN CONSENT. CONTRAVENTION WILL BE PROSECUTED

- FIGURED DIMENSIONS TO BE TAKEN IN PREFERENCE TO SCALE.
- BUILDERS' WORK TO COMPLY WITH THE LATEST BCA AND ITS AMENDMENTS AND RELEVANT AUSTRALIAN STANDARDS REFERRED WITHIN.

No.	Description	Date



Building Design | 3D Modeling | Drafting | Detailing



Accreditation No: 6302
Shop 6A/80 Thorney Rd, Fairfield West
0414 891 998 - Le@LTDesign.net.au

DRAWING:
SECTION

CLIENT & PROJECT: LOT 21 IN DP 30370
PROPOSED SECONDARY DWELLING
AT: NO. 5 JOSEPH STREET, BLACKTOWN, NSW 2148

COMPLYING DEVELOPMENT CERTIFICATE


DATE:
15/04/2026
DWG NO:
GF-0626-04



DRW BY:
LT

SCALE: 1 : 100 (A3)




JOSEPH STREET

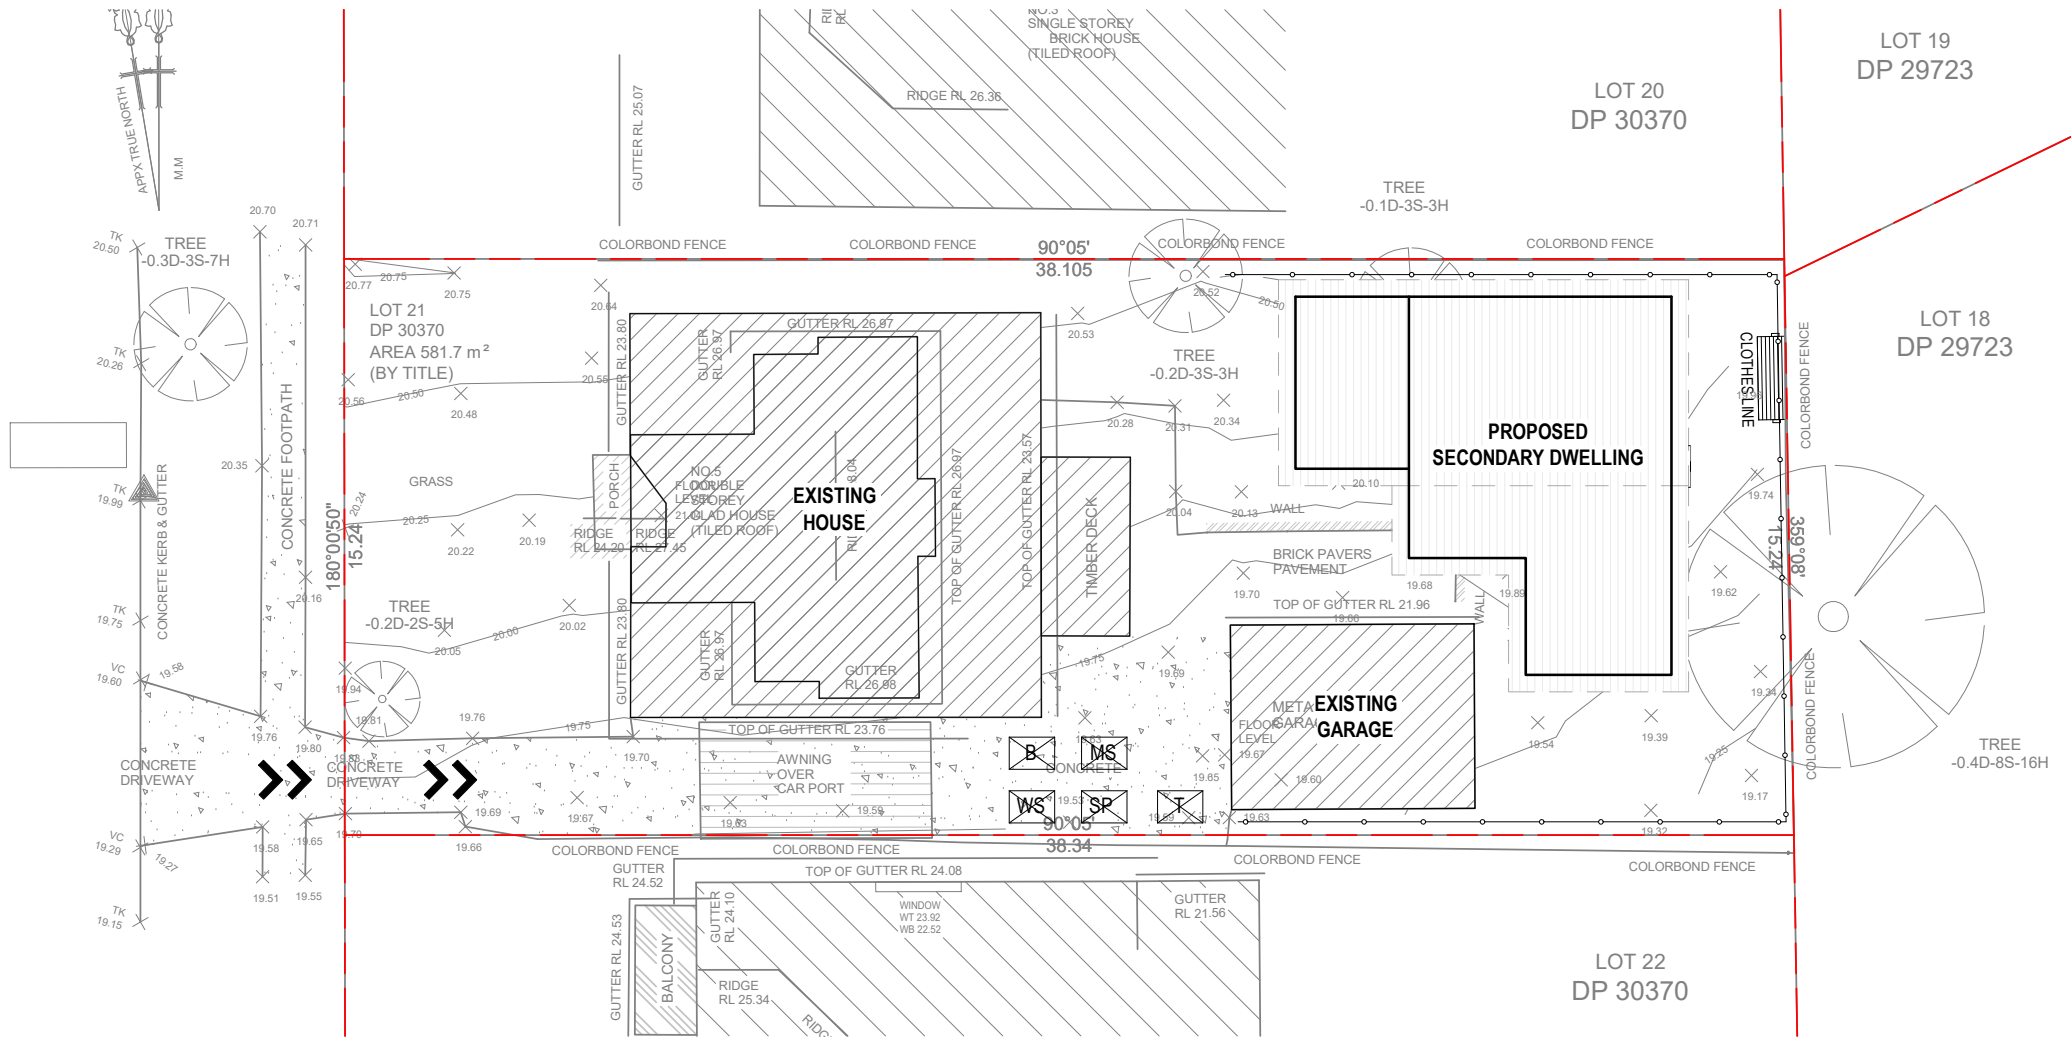

GENERAL LEGEND

- SILT FENCE
- STOCKPILE
- MATERIAL STORAGE
- WASTE STORAGE & RECYCLING AREA
- GARBAGE BIN
- ONSITE TOILET
- ACCESS FOR VEHICLES

1 EROSION & SEDIMENT CONTROL PLAN
1 : 200

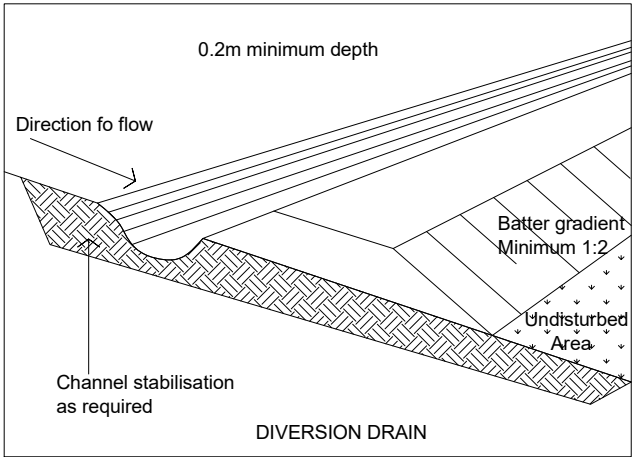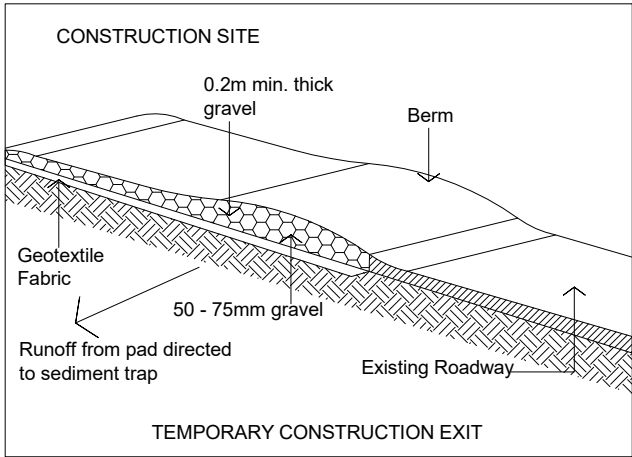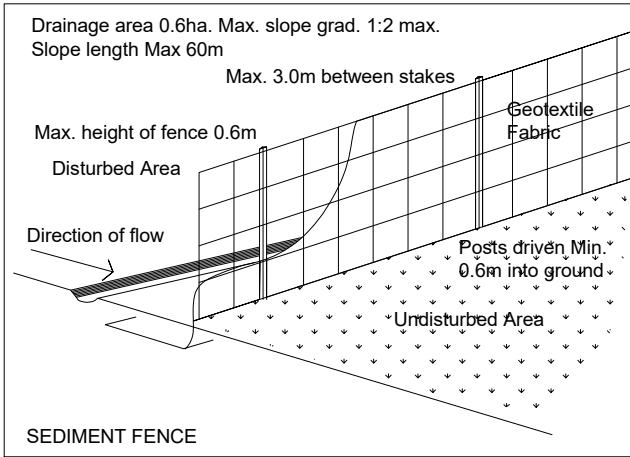

NOTES

1. NO VEHICLE CROSSING OR STOCKPILING OF MATERIAL SHOULD OCCUR ON THE VEGETATED BUFFER.
2. ALL SEDIMENT CONTROL STRUCTURES SHOULD BE INSPECTED & MAINTAINED BY THE SITE MANAGE DAILY
3. ALL SEDIMENT RETAINING STRUCTURES SHOULD BE CLEANED ON REACHING 50% STORAGE CAPACITY. SEDIMENT REMOVED SHOULD BE SPREAD WITHIN THE DISTURBED AREA.
4. ALL EXISTING VEGETATION ON THE SITE PERIMETER MUST BE RETAINED.
5. ROOF GUTTERS AND DOWNPIPES MUST BE CONNECT TO THE SITE DRAINAGE IMMEDIATELY AFTER ROOF CONSTRUCTION.
6. ALL DISTURBED AREA ARE TO BE RE-VEGETATED OR STABILISED TO PREVENT EROSION. I.E. LANDSCAPING/ MULCHING/ TURFING.
7. MATERIALS AREA NOT TO BE STORED ON THE FOOTPATH.

© THIS DRAWING IS THE PROPERTY OF LT DESIGN & CONSULTING PTY LTD AND WE RESERVE THE COPYRIGHT TO ALL OUR DESIGNS WHICH CANNOT BE REPRODUCED (IN PART OR IN WHOLE) BEFORE FIRST OBTAINING WRITTEN CONSENT. CONTRAVENTION WILL BE PROSECUTED

- FIGURED DIMENSIONS TO BE TAKEN IN PREFERENCE TO SCALE.
- BUILDERS' WORK TO COMPLY WITH THE LATEST BCA AND ITS AMENDMENTS AND RELEVANT AUSTRALIAN STANDARDS REFERRED WITHIN.

No.	Description	Date



DESIGN



BUILDING DESIGNERS AUSTRALIA

Accreditation No: 6302
Shop 6A/80 Thorney Rd, Fairfield West
0414 891 998 - Le@LTDesign.net.au

Building Design | 3D Modeling | Drafting | Detailing

DRAWING:

EROSION & SEDIMENT CONTROL PLAN

CLIENT & PROJECT: LOT 21 IN DP 30370

PROPOSED SECONDARY DWELLING

AT: NO. 5 JOSEPH STREET, BLACKTOWN, NSW 2148

COMPLYING DEVELOPMENT CERTIFICATE

DATE: 15/04/2026

DWG NO: GF-0626-05

SCALE: As indicated (A3)

DRW BY: LT

CERTIFICATE NO: 1843097S

"The specifications provided below outline water, thermal performance, material, and energy commitments as per the BASIX certificate. Any discrepancies between the drawings, this summary table, and the original BASIX certificate must be reported immediately to the designer. Always refer to the original BASIX certificate for building construction, materials, insulation requirements, and other details. Please do not solely rely on this summary table, as it only highlights the essential criteria for the purpose of approval."

WATER COMMITMENTS

Showerheads Sytem: Min. 4 star Kitchen Taps: Min. 3 star
Toilet Flushing Sysmtem: Min. 3 star Basin Taps: Min. 3 star
Rainwater Tank: 2000 litres & connect to all the toilets

THERMAL PERFORMANCE AND MATERIALS COMMITMENTS

EXTERNAL WALLS

Material: External Wall Cladding Insulation: R2.5 (or 3.0 incl. const.)
Wall Colour: Light

INTERNAL WALLS

Materials: Plasterboard on Timber Wall Frame

WINDOWS

Glazing: Clear Glazing Frame : Standard Aluminium Internal cover: Blinds
Eaves: 450mm Window Frame / Glass Specs: Ref. to Basix for details

ROOF

Material: Colorbond Roof Type: Flat Roof - 5 Degrees
Roof Colour: Medium (solar absorptance 0.48- 0.59) Insulation: foil/sarking

CEILINGS


Material: Plasterboard Insulation: R4 (up)
Ceiling Fan: in living room

FLOORS

Covering: not specified Materials: Concrete Insulation: NIL

ENERGY COMMITMENTS

Hotwater unit : Gas Instantaneous - 5 STARS
Cooling / Heating System: A/C System 3 star
Ventilation System: Mechanical Vent. System to Kitchen, Bathroom and Laundry
Outdoor Clothes Drying

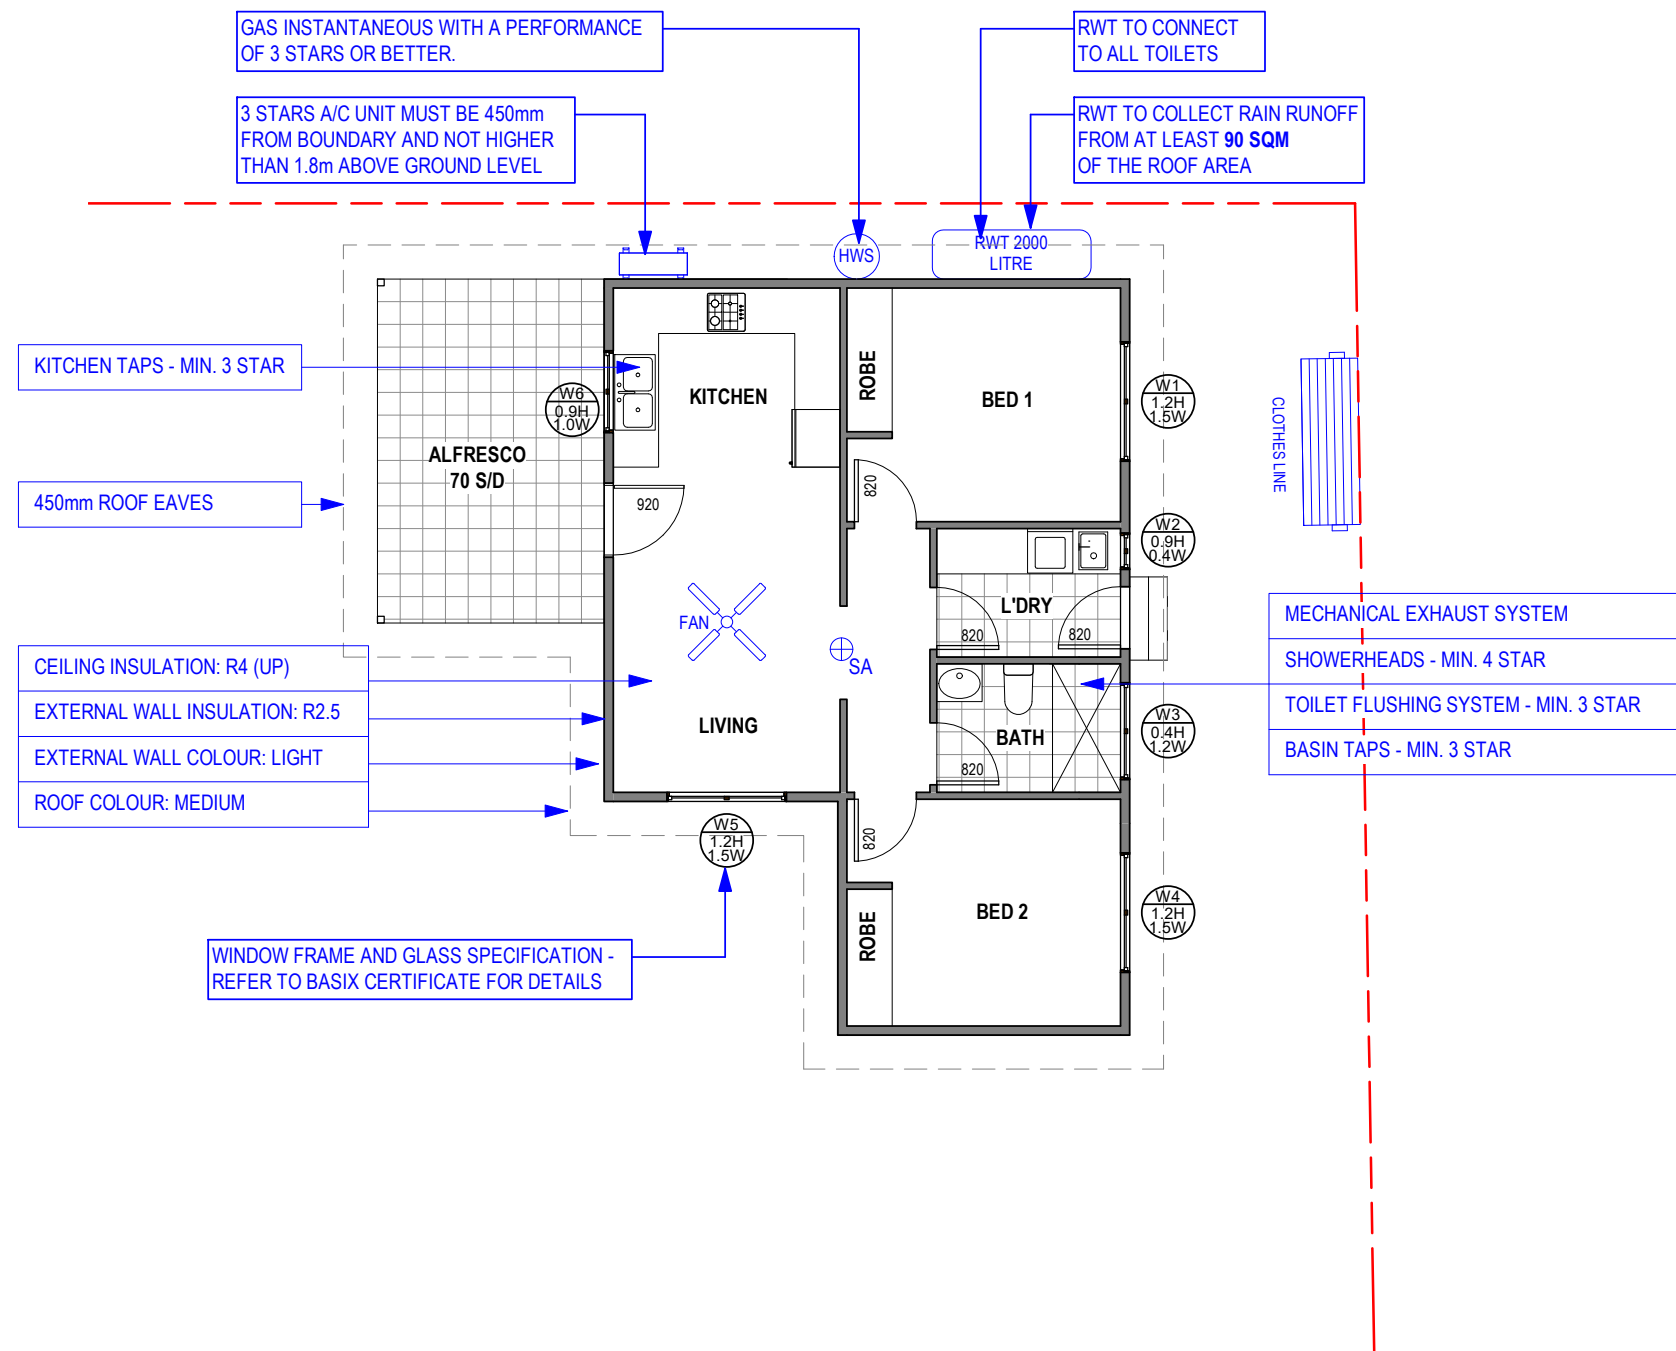

1 PROPOSED GROUND FLOOR PLAN
1 : 100

© THIS DRAWING IS THE PROPERTY OF LT DESIGN & CONSULTING PTY LTD AND WE RESERVE THE COPYRIGHT TO ALL OUR DESIGNS WHICH CANNOT BE REPRODUCED (IN PART OR IN WHOLE) BEFORE FIRST OBTAINING WRITTEN CONSENT. CONTRAVENTION WILL BE PROSECUTED

• FIGURED DIMENSIONS TO BE TAKEN IN PREFERENCE TO SCALE.

• BUILDERS' WORK TO COMPLY WITH THE LATEST BCA AND ITS AMENDMENTS AND RELEVANT AUSTRALIAN STANDARDS REFERRED WITHIN.

No.	Description	Date



Building Design | 3D Modeling | Drafting | Detailing



BUILDING
DESIGNERS
AUSTRALIA

Accreditation No: 6302
Shop 6A/80 Thorney Rd, Fairfield West
0414 891 998 - Le@LTDesign.net.au

DRAWING:

BASIX COMMITMENTS PLAN

CLIENT & PROJECT: LOT 21 IN DP 30370

PROPOSED SECONDARY DWELLING
AT: NO. 5 JOSEPH STREET, BLACKTOWN, NSW 2148

COMPLYING DEVELOPMENT CERTIFICATE

DATE:
15/04/2026






DWG NO:
GF-0626-06

SCALE:




DRW BY:
LT

As indicated (A3)

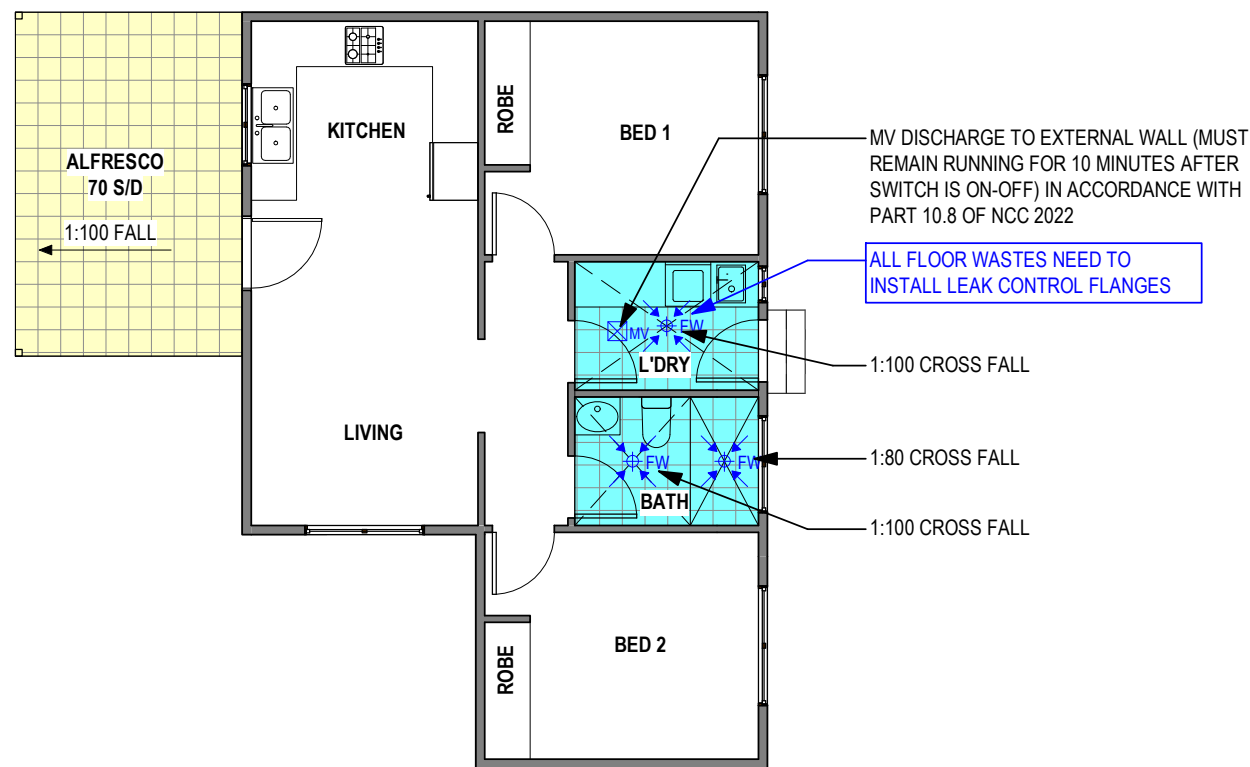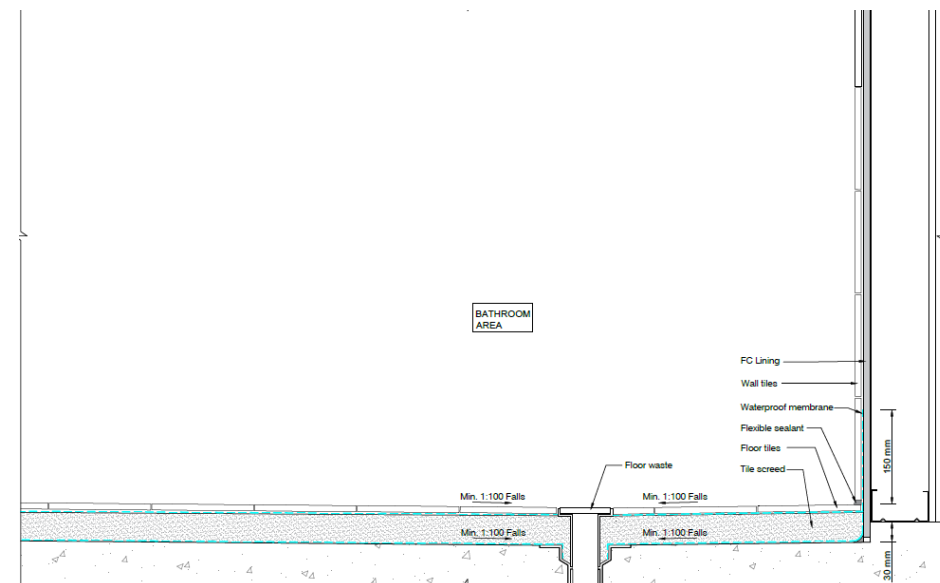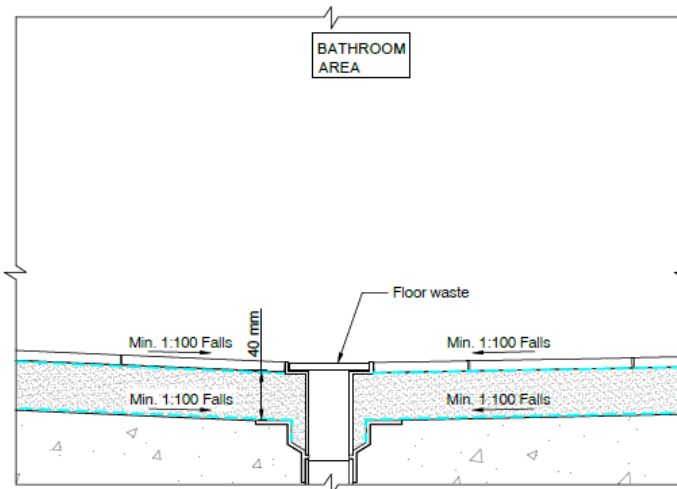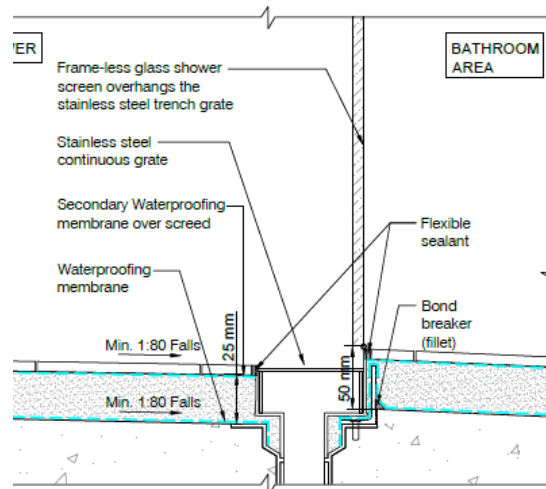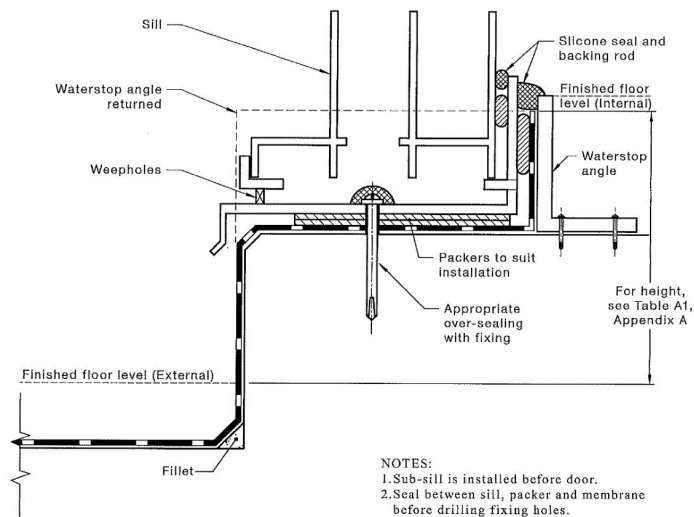

1 PROPOSED GROUND FLOOR PLAN
1 : 100

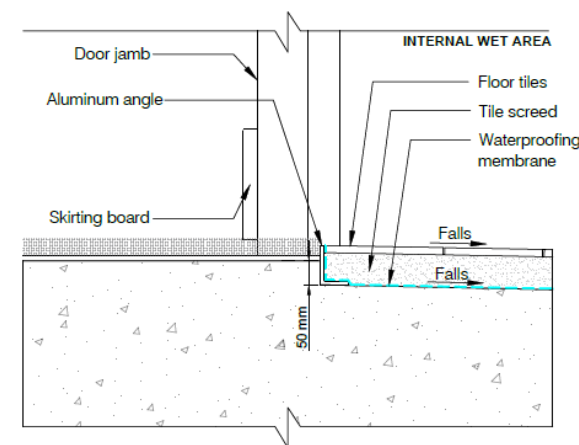

INTERNAL WET AREA DOOR THRESHOLD

LEGEND:

- WATERPROOFING TO INTERNAL WET AREA AS PER AS 3740
- WATERPROOFING TO EXTERNAL WET AREA AS PER AS 4654 (BALCONIES ONLY)
- WATERPROOFING TO EXTERNAL WET AREA AS PER AS 4654
- WATERPROOFING TO PLANTER BOX

© THIS DRAWING IS THE PROPERTY OF LT DESIGN & CONSULTING PTY LTD AND WE RESERVE THE COPYRIGHT TO ALL OUR DESIGNS WHICH CANNOT BE REPRODUCED (IN PART OR IN WHOLE) BEFORE FIRST OBTAINING WRITTEN CONSENT. CONTRAVENTION WILL BE PROSECUTED

- FIGURED DIMENSIONS TO BE TAKEN IN PREFERENCE TO SCALE.
- BUILDERS' WORK TO COMPLY WITH THE LATEST BCA AND ITS AMENDMENTS AND RELEVANT AUSTRALIAN STANDARDS REFERRED WITHIN.

No.	Description	Date



Building Design | 3D Modeling | Drafting | Detailing



Accreditation No: 6302
Shop 6A/80 Thorney Rd, Fairfield West
0414 891 998 - Le@LTDesign.net.au

DRAWING:
WET AREAS PLAN

CLIENT & PROJECT: LOT 21 IN DP 30370
PROPOSED SECONDARY DWELLING
AT: NO. 5 JOSEPH STREET, BLACKTOWN, NSW 2148

COMPLYING DEVELOPMENT CERTIFICATE


DATE:
15/04/2026
DWG NO:
GF-0626-07

DRW BY:
LT


SCALE: 1 : 100 (A3)



NOTES:
ALL WATERPROOFING
MUST BE COMPLIED WITH:
- AS 3740:2021
- NCC 2022 - VOLUME 2 -
HOUSING PROVISIONS

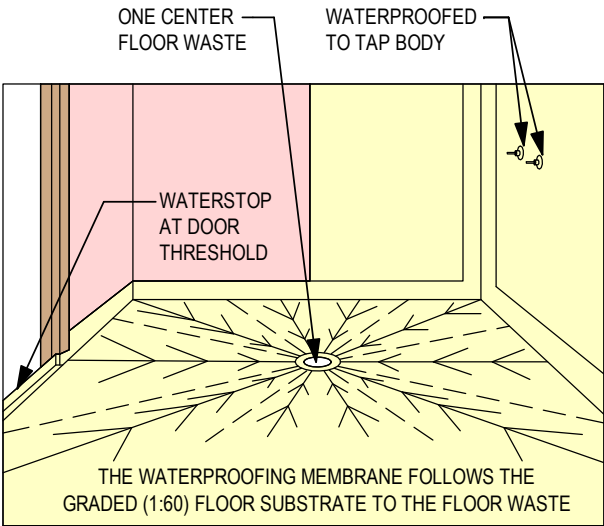

C01 CROSS FALL TO FLOOR WASTE

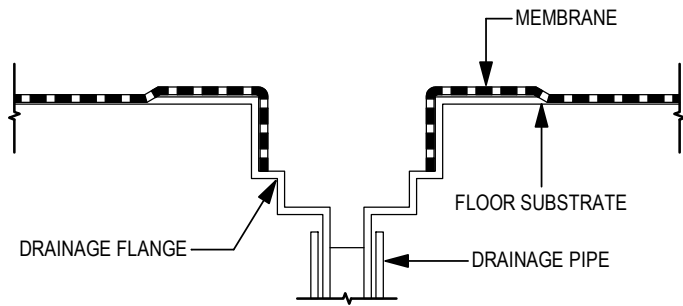


TYPICAL MEMBRANE TERMINATION
AT DRAINAGE OUTLET
NOT TO SCALE

C02 LEAK CONTROL FLANGES




PUDDLE / LEAK CONTROL
DRAINAGE FLANGES


NOTE: MUST BE APPLIED TO ALL FLOOR WASTES IN WET AREA FOR
GROUND AND UPPER FLOOR / ENTIRE BUILDING
(CLASS 1 BUILDING: CONCRETE FLOOR - MAY SIT ON TOP OF
CONCRETE OR TILE BED FOR - CONCRETE FLOOR ONLY,
OTHER FLOORS - RECESSED INTO FLOOR SUBTRATE OR TILE BED)

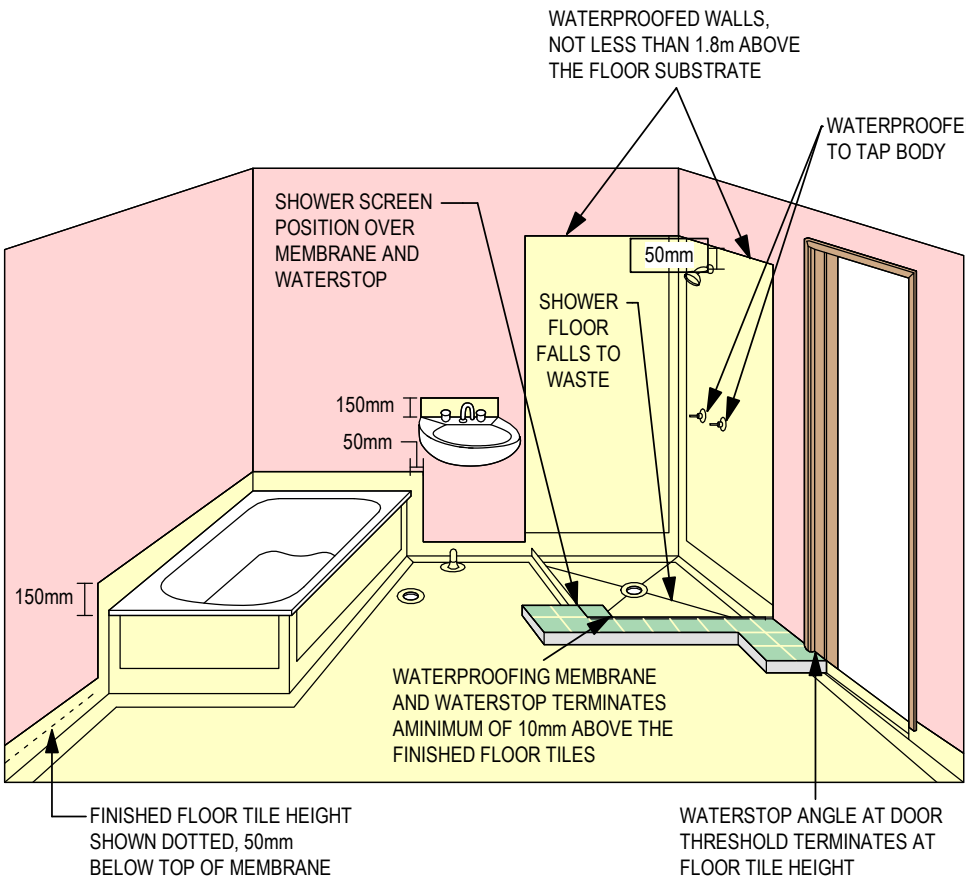

C03 WATERPROOFING DETAILS AROUND BATHROOM

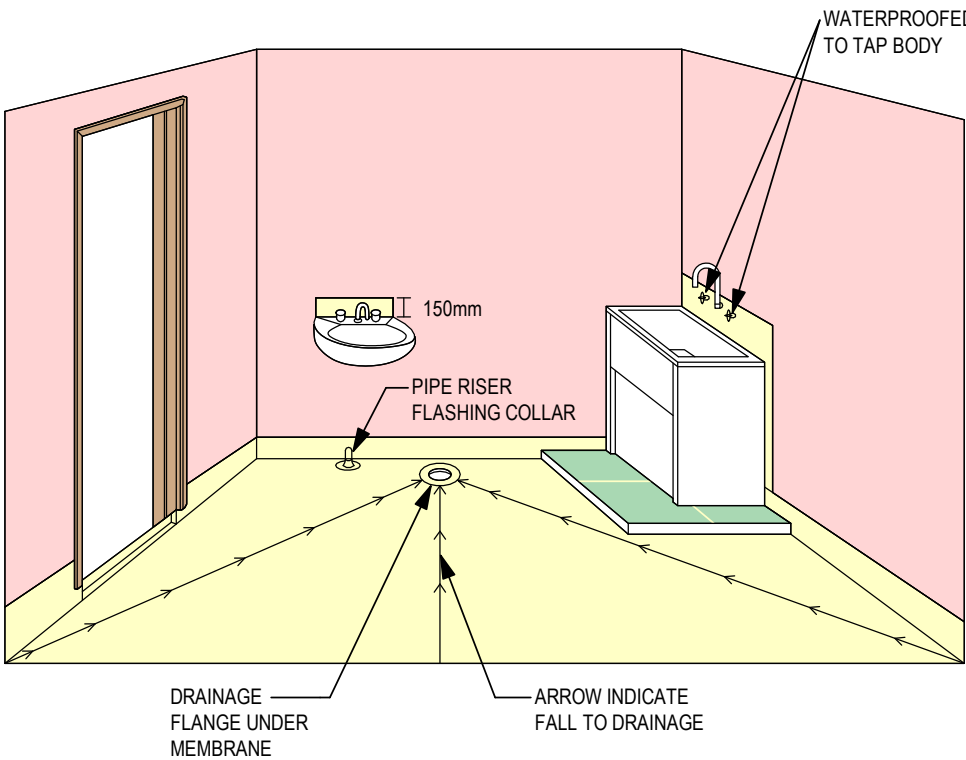

C04 WATERPROOFING DETAILS AROUND LAUNDRY

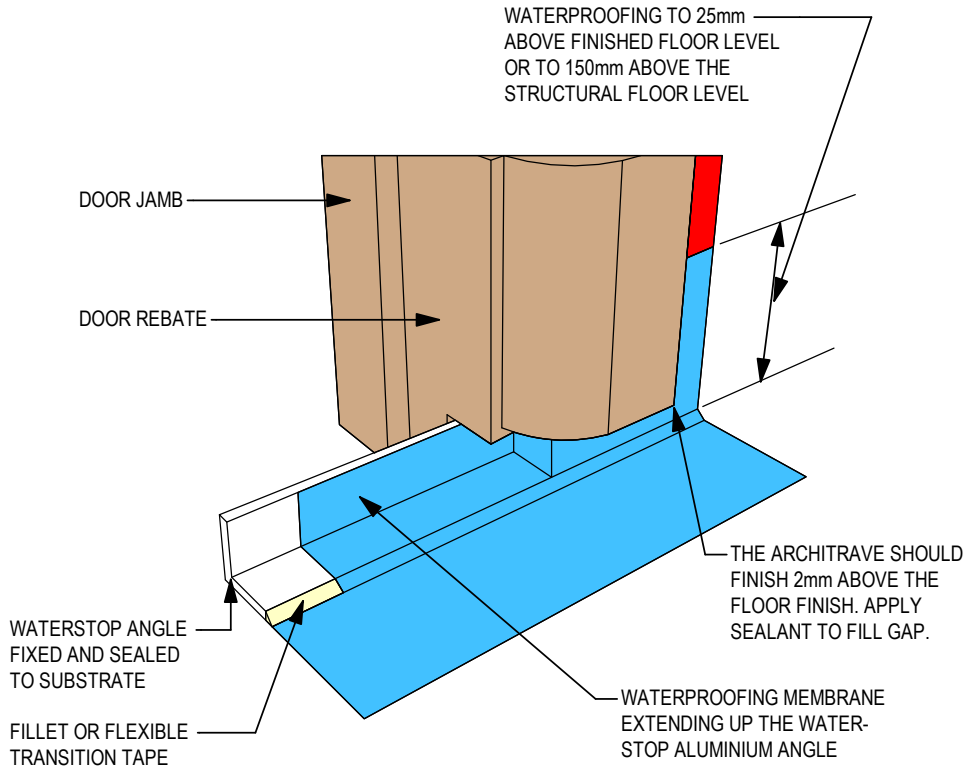

NOTE: THE WATERSTOP ANGLE MAY BE LOCATED AT
THE FACE OF THE DOOR JAMP OR AT THE REBATE.

C05 WATERPROOFING UNDER DOOR ARCHITRAVE

© THIS DRAWING IS THE PROPERTY OF LT DESIGN & CONSULTING PTY LTD AND WE RESERVE THE COPYRIGHT TO ALL OUR DESIGNS WHICH CANNOT BE REPRODUCED (IN PART OR IN WHOLE) BEFORE FIRST OBTAINING WRITTEN CONSENT. CONTRAVENTION WILL BE PROSECUTED

- FIGURED DIMENSIONS TO BE TAKEN IN PREFERENCE TO SCALE.
- BUILDERS' WORK TO COMPLY WITH THE LATEST BCA AND ITS AMENDMENTS AND RELEVANT AUSTRALIAN STANDARDS REFERRED WITHIN.

No.	Description	Date



Building Design | 3D Modeling | Drafting | Detailing



Accreditation No: 6302
Shop 6A/80 Thorney Rd, Fairfield West
0414 891 998 - Le@LTDesign.net.au

DRAWING:
TYPICAL WATERPROOFING CONSTRUCTION DETAILS

CLIENT & PROJECT: LOT 21 IN DP 30370
PROPOSED SECONDARY DWELLING
AT: NO. 5 JOSEPH STREET, BLACKTOWN, NSW 2148

COMPLYING DEVELOPMENT CERTIFICATE

DATE:
15/04/2026
DWG NO:
GF-0626-08

DRW BY:
LT

SCALE: 1 : 5 (A3)

