

LOT 9 54 HONEYSUCKLE
PARADE MARSDEN PARK 2765

PROPOSED DOUBLE STOREY ATTACHED DUAL
OCCUPANCY



PERSPECTIVE VIEW

ALL DESIGN AND CONSTRUCTION IN ACCORDANCE WITH BUILDING CODE
OF AUSTRALIA AND ALL CURRENT AUSTRALIAN STANDARDS, OH&S, WORK
COVER, EPA, LOCAL COUNCIL APPROVALS AND REQUIREMENTS.
ALL DRAWINGS ARE TO BE READ IN CONJUNCTION WITH BASIX CERTIFICATE

AUSTRALIAN STANDARDS COMPLIANCE:
The building works shall be constructed in accordance with, but not limited to, the following Australian Standards.

Site preparation
- **Termite risk Management** - Termite management system to be provided in accordance with HP Part 3.5 and AS 3660.1 and/or AS 3660.3

- **Drainage** - Drainage to site to comply with HP Part 3.3 OR AS/NZS 3500.3 in accordance with NCC 2022 H2D2.

Masonry
- **Vertical articulation joints** - Masonry articulation joints to be provided as specified in HP 5.6.8 or AS 4773.2 or AS 3700.

Framing
- **Frame** - Timber Frames & Trusses - Designed and constructed to AS/NZS 1170.1 - 2002, AS/NZS 1170.2 - 2021, AS 1684.2 - 2021, AS 1720.1 - 2010, AS 1720.5 - 2015 and AS 4440 -2004 - Installation of nailplated timber roof trusses.

- **Frame** - Steel Frames - Designed and constructed to NASH Part 1 & 2, AS 4100 & AS/NZS 4600.

- **Subfloor ventilation** - Sub-floor ventilation and clearance compliance with NCC Housing Provisions Part 6.2.

Roof and wall cladding
- **Gutters & downpipes** - Downpipes & Gutters to comply with NCC Housing Provisions Part 7.4 OR AS/NZS 3500.3.

- **Timber and composite wall cladding** - Cladding material to be in accordance with HP Part 7.5 OR for AAC-AS 5146.1 OR for metal wall cladding AS 1562.1.

- **Roof and wall cladding** - All Roof and wall cladding to be designed and installed in accordance with NCC 2022 H1D7.

Glazing
- **Glazing** - All glazing to be in accordance with H1D8 & H2D7 of the NCC Volume Two, Section 8 of the Housing Provisions & Australian Standards AS 1288, 2047, 4055. (Basic requirements to be addressed also)

Health and amenity
- **Wet area waterproofing** - Wet area in accordance with H4D1, H4D2 & H4D3 of the NCC Volume Two and Part 10.2 of the Housing Provisions OR Clauses 10.2.1 to 10.2.6 & 10.2.12 and AS 3740.

- **Floor Waste** - Wet Area - All provided floor waste to have floor falls to them between 1:50 - 1:80 as per NCC Housing Provisions Clause 10.2.12.

- **External waterproofing** - External waterproofing for roofing systems on flat roofs, roof terraces, balconies and terraces and other similar horizontal surfaces located above internal spaces of a building compliant with NCC Volume 2 H2D8 & AS 4654.1 & 2.

Condensation management
- **External wall construction** - Where pliable building membrane is installed in an external wall it is comply with HP 10.8.1 and AS 4200.1 & 2.

- **Exhaust systems** - The bathroom &/or sanitary compartment/s with an exhaust system and NOT provided with compliant natural ventilation must be interlocked to rooms light switch and have off timer set for 10 minutes after the light is switched off.

- **Exhaust systems** - The rooms with an exhaust system and not provided with compliant natural ventilation must be provided with make-up air from adjacent room of 14,000mm² which is approx. a 20mm undercut of a 700mm door or 18mm from an 820mm door.

- **Exhaust systems** - The exhaust system installed in a kitchen, bathroom, sanitary compartment or laundry must have a minimum flow rate of- (a) 25 L/s for a bathroom or sanitary compartment; and (b) 40 L/s for a kitchen or laundry.

- **Ventilation of roof spaces** - In climate zones 6, 7 & 8 a roof space must be ventilated in accordance with HP Part 10.8.3.

Safe movement and access
- **Stairway and ramp construction** - Stairways and ramps to be constructed to HP Part 11.2.

- **Barrier and handrails** - Barrier and handrails to be constructed to HP Part 11.3.

- **Barrier and handrails** - Handrail to stairways having a change in elevation exceeding 1m required to be provided at a height not less than 865mm to NCC Housing Provisions Clause 11.3.5.


- **Barrier and handrails** - Bedroom windows where the FFL is 2m or more above the surface beneath are to have window restrictors OR screens (crim-safe style mesh) installed as per NCC Housing Provisions Clause 11.3.7.

- **Barrier and handrails** - Windows other than bedroom with FFL 4m or more above adjacent surface to have sill or barrier minimum 865mm above FFL as per NCC Housing Provisions Clause 11.3.8.

WE RELY ON SURVEY PROVIDED FOR SITE BOUNDARIES , LEVELS, EASEMENTS , SERVICES ETC.
OWNER SHOULD CHECK ANY INCONSISTENCIES PRIOR TO COMENCEMENT OF ANY WORK ON SITE.


WE RELY ON SURVEY PROVIDED FOR SITE BOUNDARIES , LEVELS, EASEMENTS , SERVICES ETC.

OWNER SHOULD CHECK ANY INCONSISTENCIES PRIOR TO COMENCEMENT OF ANY WORK ON SITE.

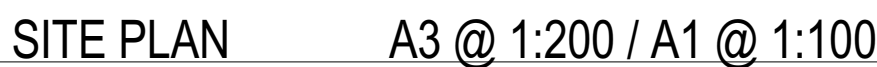

UNIT 2	
AREA CALCULATION	
SITE	153.10m ²
PORCH	3.96m ²
GARAGE	19.42m ²
GROUND LIVING	48.54m ²
ALFRESCO	10.41m ²
FIRST LIVING	76.97m ²
BALCONY	3.60m ²
TOTAL	162.90m ²
	17.52SQ
GFA	107.63m ²

300 A1 PAPER mm DWG (m) @ 1:100 0 1 5 10 20
150 A3 PAPER mm DWG (m) @ 1:150 1 5 10 20
200 100
100 50
50 25
0 10 5 mm

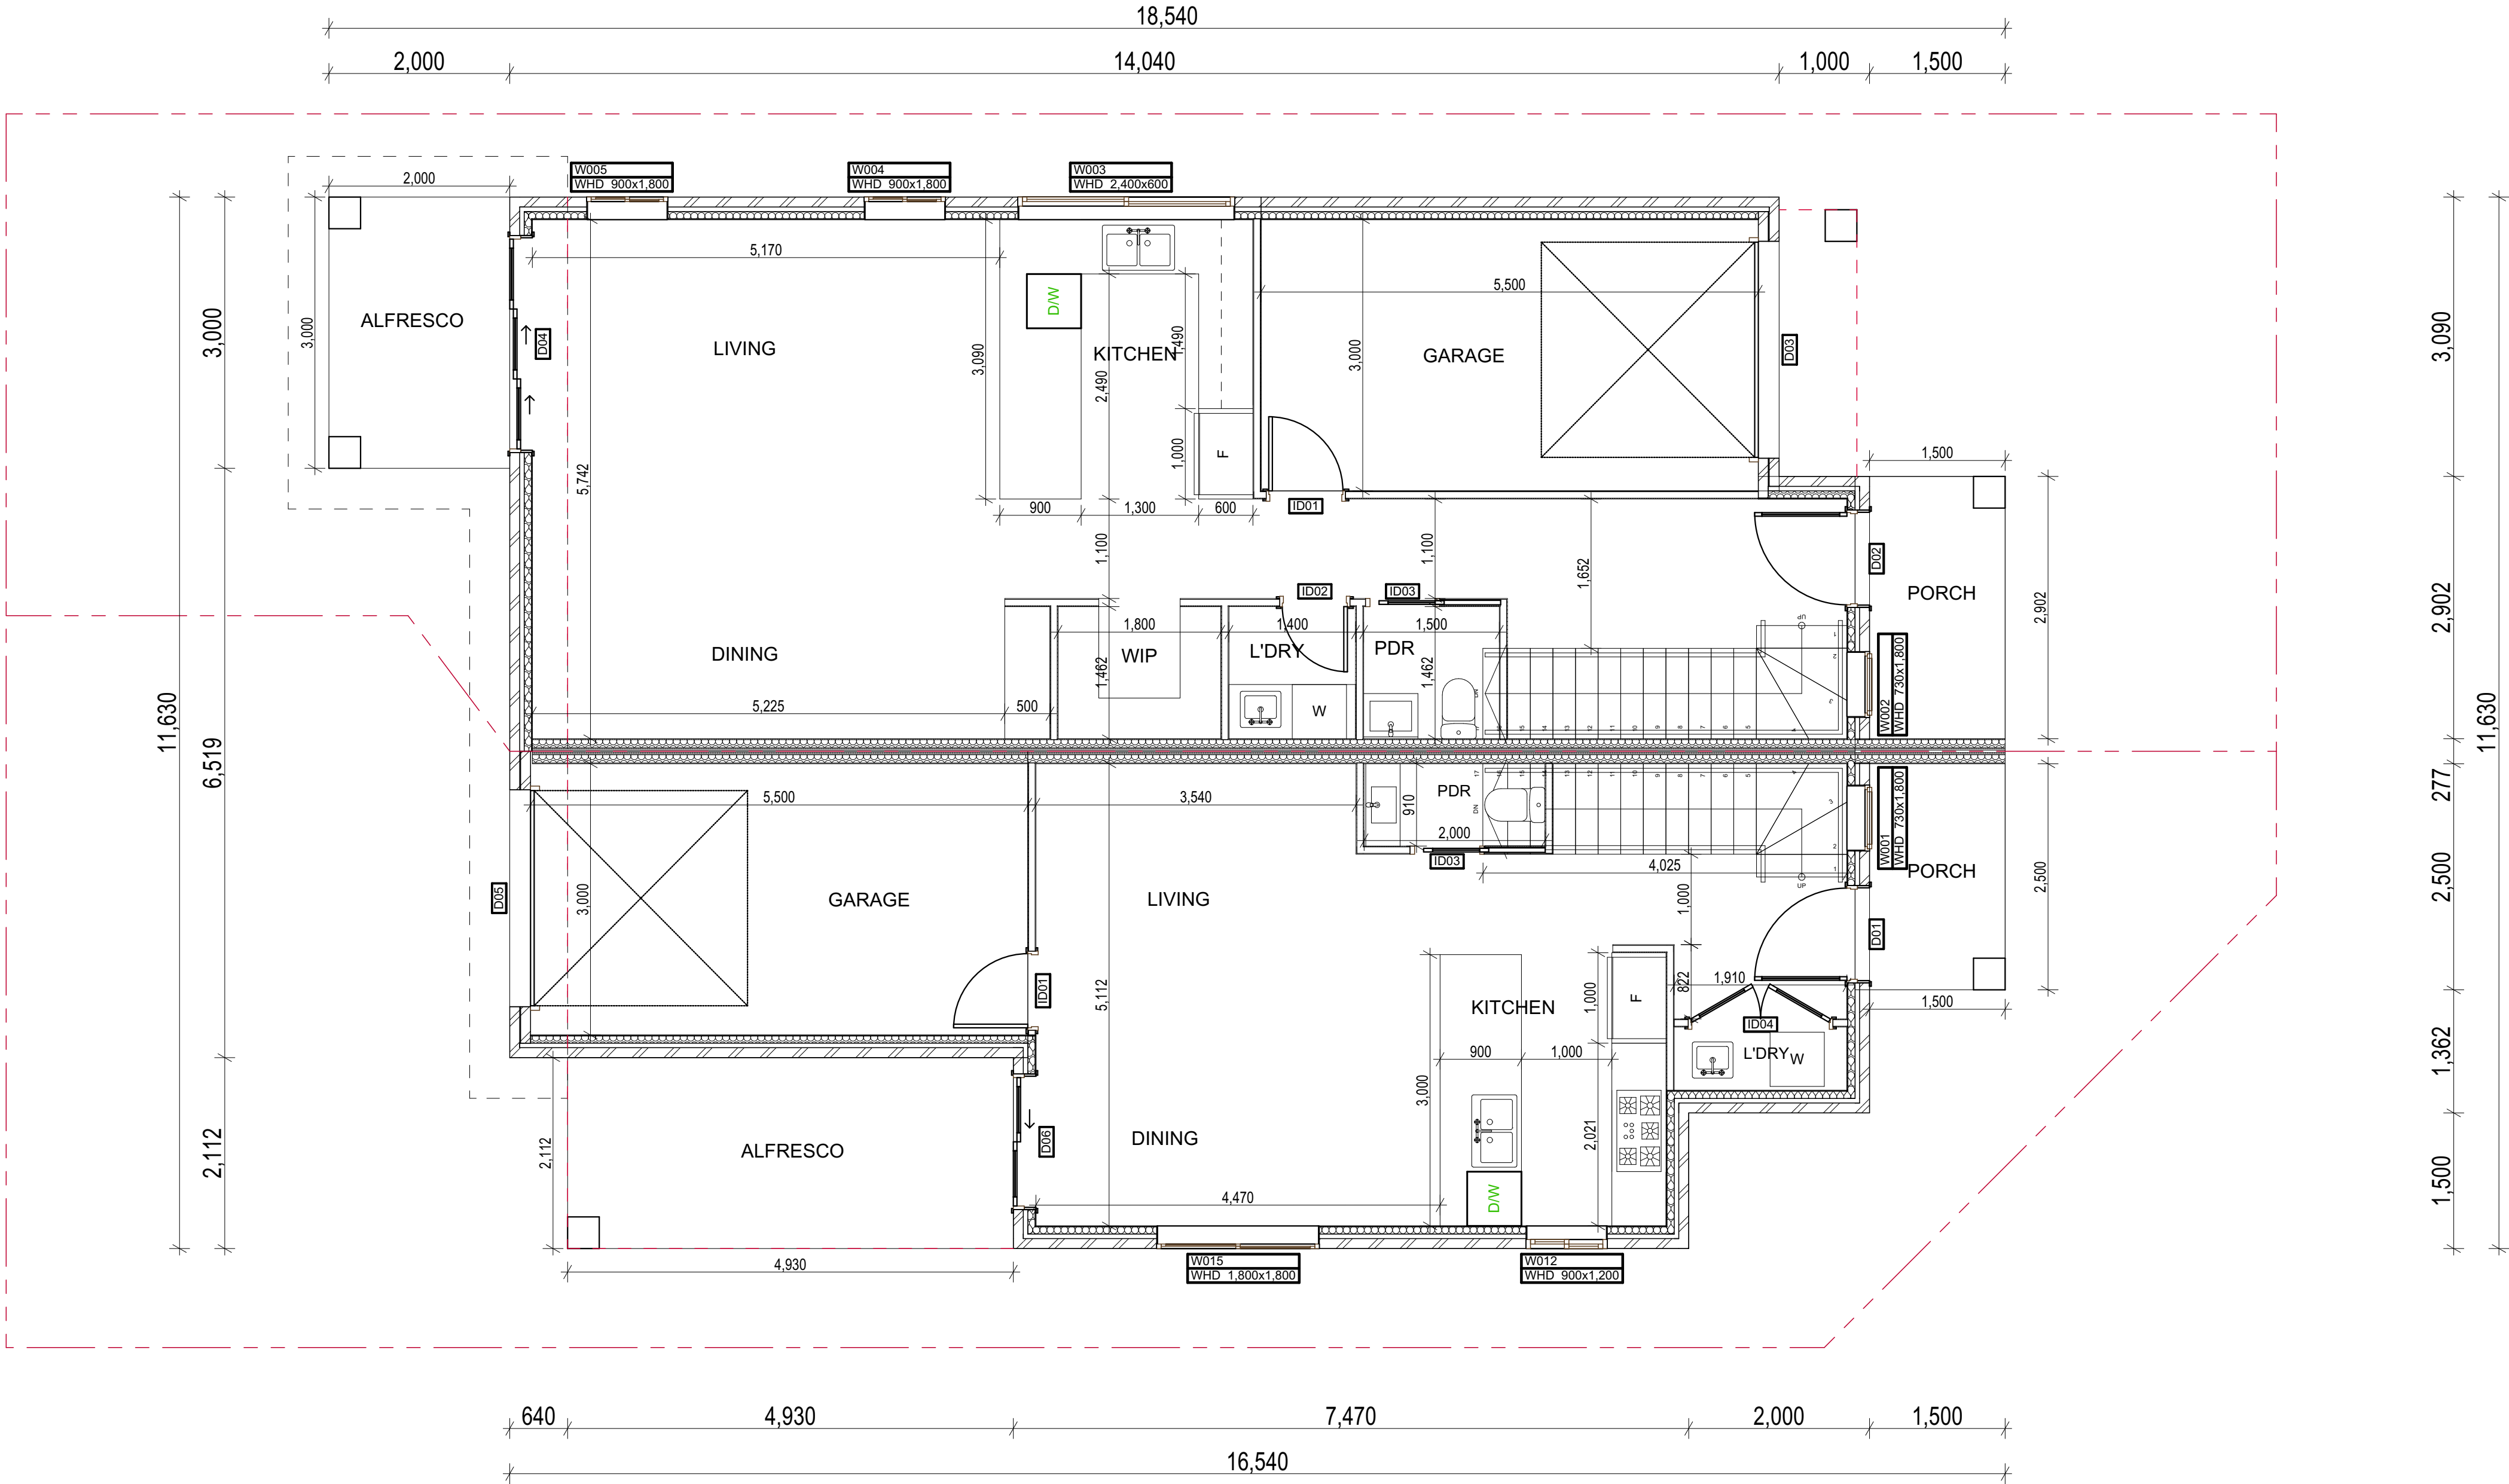

GROUND FLOOR A3 @ 1:100 / A1 @ 1:50

300 A1 PAPER mm DWG (m) @ 1:100 0 1 5 10 20
150 A3 PAPER mm DWG (m) @ 1:50 m
200 100
100 50
50 25
0 mm 5



EMAIL: info@nirvadesigns.com.au
PHONE: 02 800 64782
POST: PO BOX 262 Stanhope Gardens NSW 2768



1. DRAWINGS & DESIGN ARE THE INTELLECTUAL PROPERTY OF NIRVA DESIGNS
DESIGNS PTY LTD. THEY MUST NOT BE USED OR REPRODUCED WITHOUT WRITTEN CONSENT
2. ALL DIMENSIONS ARE IN MILLIMETRES UNLESS NOTED OTHERWISE
3. DO NOT SCALE DIRECTLY FROM DRAWINGS. USE WRITTEN DIMENSIONS ONLY.
4. CONFIRM ALL DIMENSIONS AND LEVELS ON SITE AND REPORT ANY DISCREPANCIES
TO DESIGNER PRIOR TO THE COMMENCEMENT OF WORK
5. ISSUED DRAWINGS MUST BE READ IN CONJUNCTION WITH ENTIRE CONTRACT SET
& CONSULTANTS DOCUMENTATION (REFER TO INDEX)


6. ENSURE ALL WORK IS UNDERTAKEN USING THE MOST RECENT ISSUE
OF DOCUMENTATION (REFER TO REVISION ISSUE & DATE)
7. REFER TO MATERIALS SCHEDULE, CONSTRUCTION SPEC, MANUFACTURES' SPEC,
AND ENGINEERS' DETAILS
8. COMPLY WITH ALL BUILDING CODES, REGULATIONS, & ORDINANCE REQUIREMENTS
9. ALL EXISTING SITE DIMENSIONS AND LEVELS ARE SUBJECT TO SURVEY
10. THESE DRAWINGS MUST NOT BE USED FOR CONSTRUCTION UNLESS SIGNED AND
ISSUED AS 'FOR CONSTRUCTION' (REFER TO REVISION ISSUE)

PROJECT: **PROJECT TITLE:**
ND2627009
SITE ADDRESS:
Lot 9 54 Honeysuckle Parade
Marsden Park NSW 2765 Australia

CLIENT: **#Client Full Name**
ISSUED AS:
SKETCH

REV: 0

FIRST FLOOR PLAN
2001 24/08/2026
C:\Users\ngam\Nirva Designs\17\Draw - 00000000
0206-27ND2627009 - 54 Honeysuckle Parade Marsden Park2
Building Plans\ND2627009 - 54 Honeysuckle Parade Marsden
Park_R01.pdf

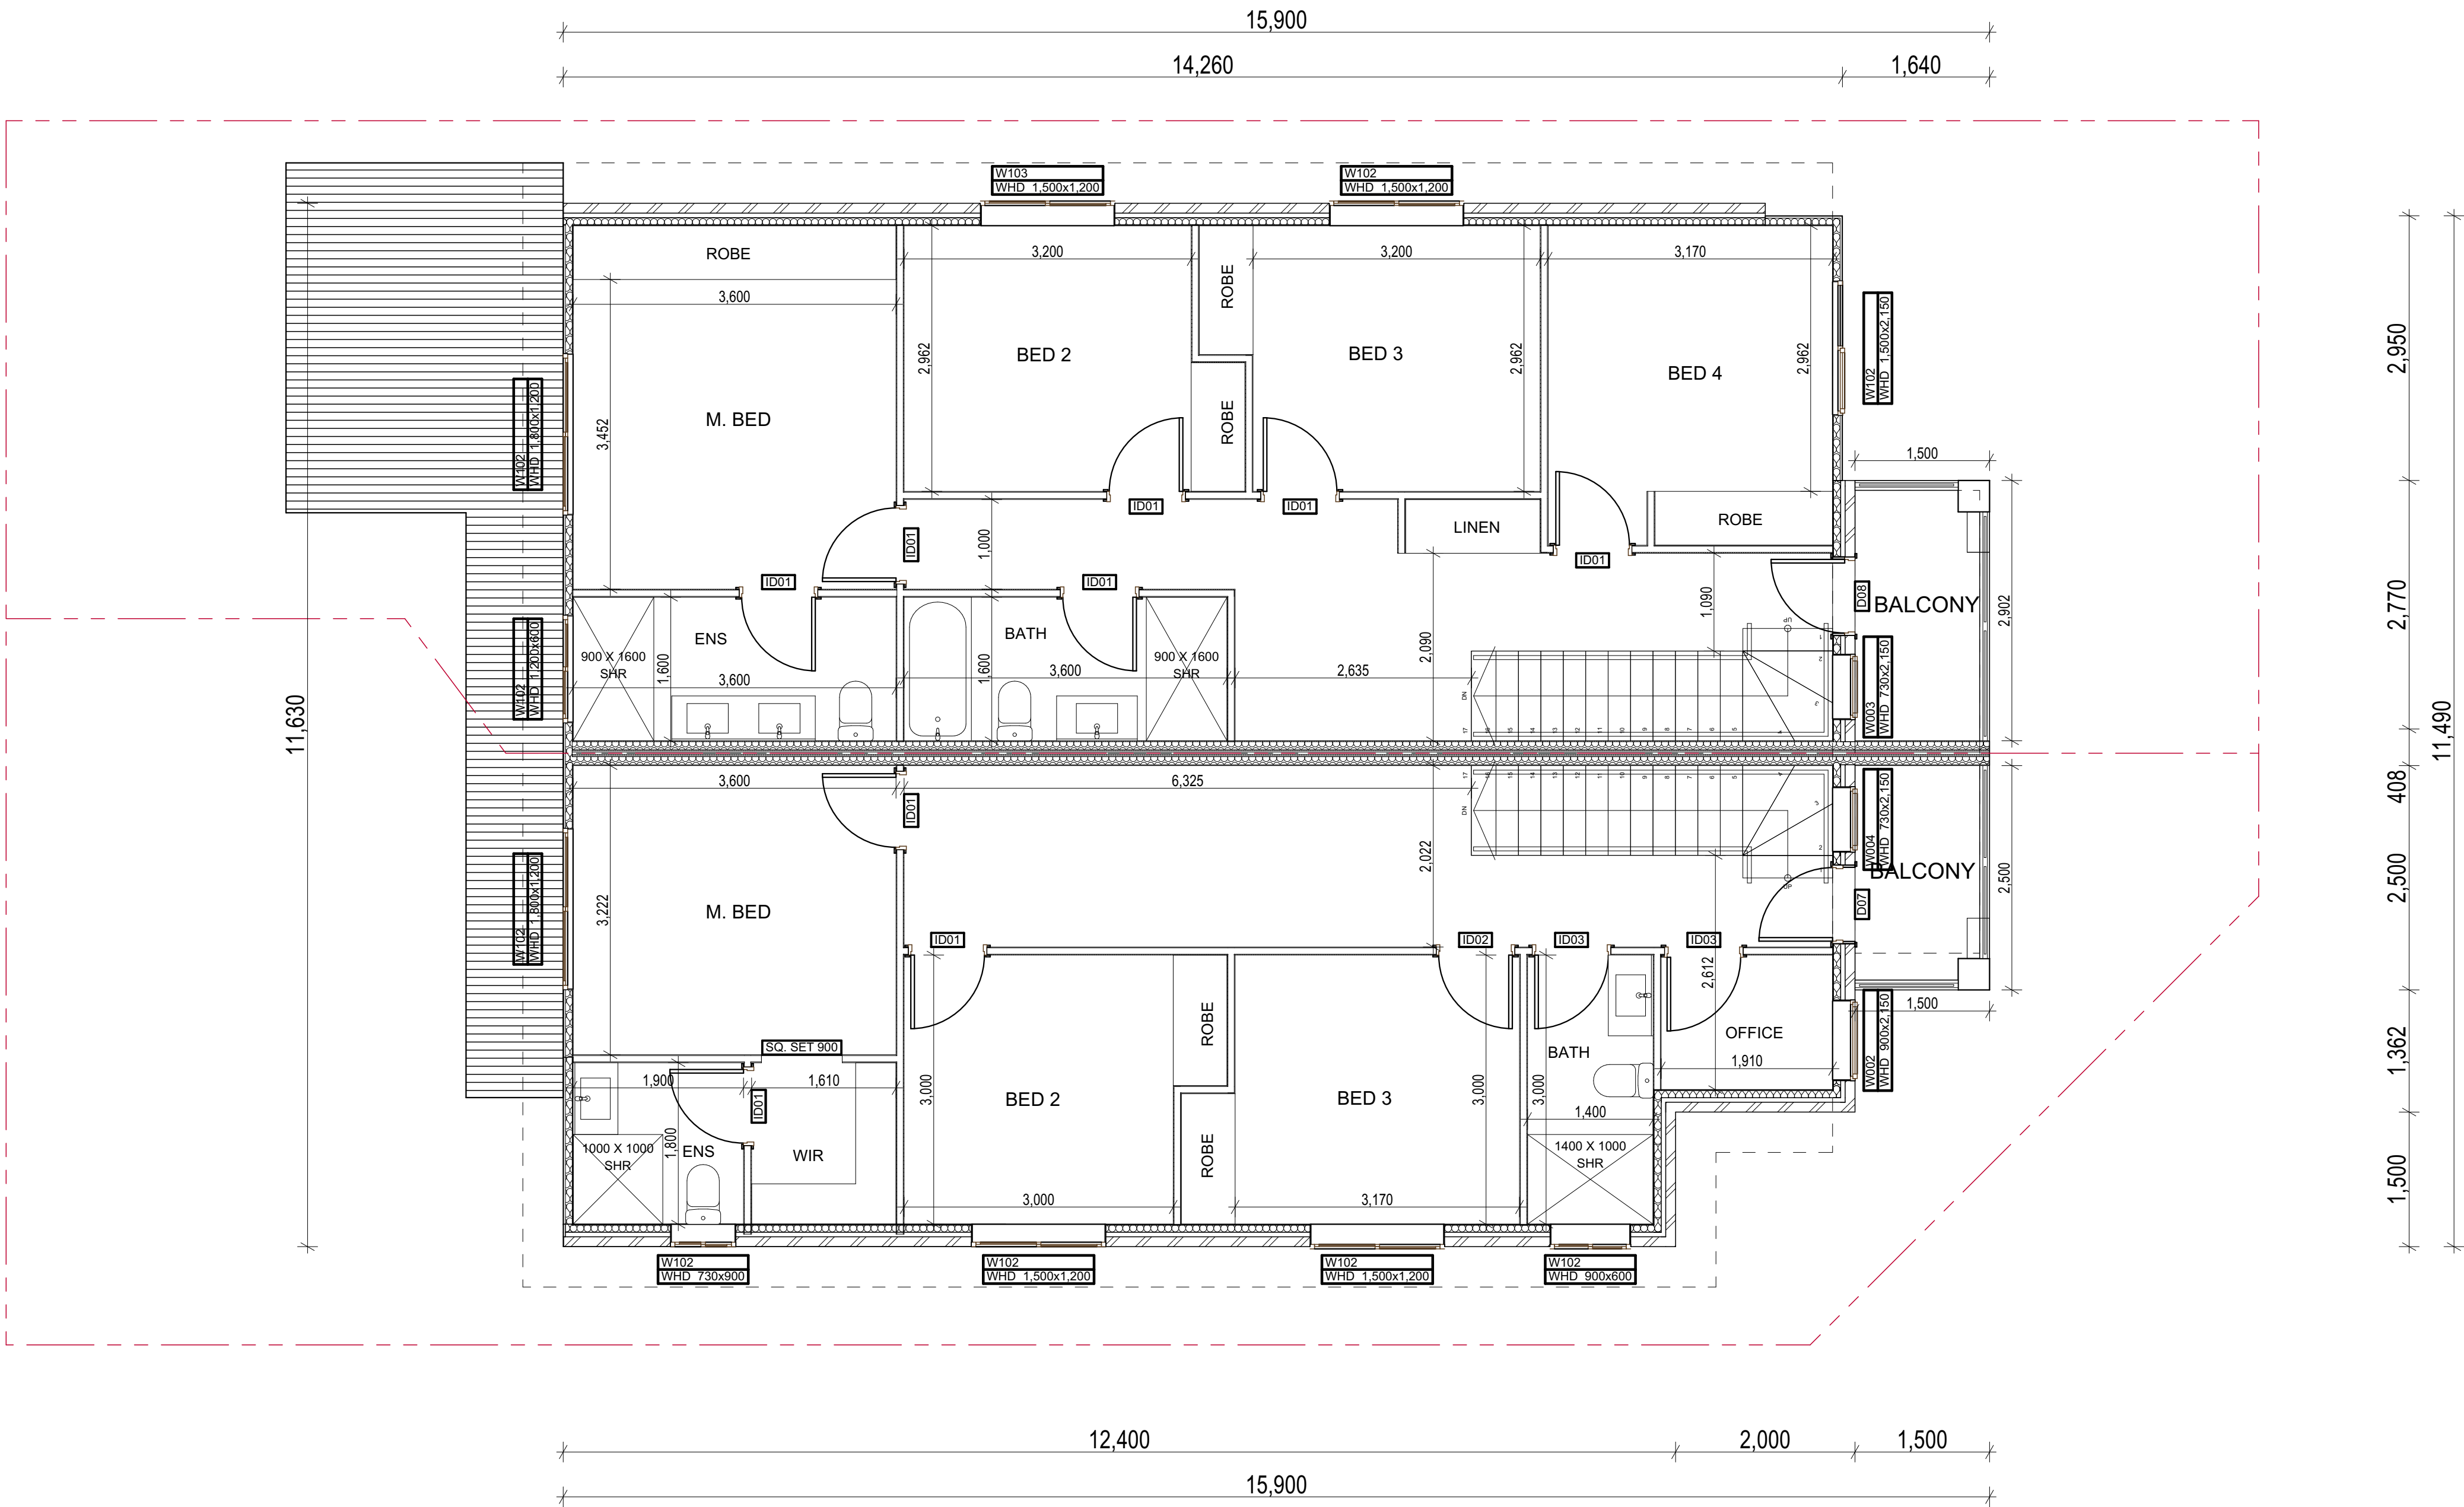

20
10
5
1
0
300 A1 PAPER mm
150 A3 PAPER mm
DWG (m) @ 1:100
DWG (m) @ 1:50
200
100
50
25
10
5
0
mm

