

1 8 T H O R P E W A Y , B O X H I L L ( L O T 5 1 5 )

- A000 - COVER SHEET
- A001 - GENERAL NOTES & BASIX
- A100 - LOCATION PLAN & SITE PLAN
- A200 - BASEMENT LEVEL PLAN
- A201 - GROUND LEVEL PLAN
- A202 - FIRST LEVEL PLAN
- A203 - ROOF PLAN
- A204 - CONCRETE SETOUT PLAN
- A300 - PROPOSED ELEVATIONS
- A301 - PROPOSED ELEVATIONS
- A302 - PROPOSED SITE ELEVATIONS
- A400 - PROPOSED SECTIONS
- A400 - PROPOSED SITE SECTIONS
- A700 - MATERIAL SCHEDULE
- A900 - SEDIMENT AND EROSION PLAN
- A901 - CUT AND FILL PLAN
- A1000- LANDSCAPE PLAN

REFER ALSO OTHER CONSULTANTS DRAWINGS:

- 1. SURVEY
- 2. STORMWATER/HYDRAULIC DRAWINGS
- 3. BASIX CERTIFICATE
- 4. LANDSCAPE DRAWINGS
- 5. STATEMENT OF ENVIRONMENTAL EFFECTS
- 6. BUSHFIRE REPORT





C O N S T R U C T I O N C E R T I F I C A T E - R E S I D E N T I A L D W E L L I N G

| REV. | DESCRIPTION                    | BY. | DATE       | NOTES   | CLIENT                                                                                       | DRAWING TITLE                        |
|------|--------------------------------|-----|------------|---|----------------------------------------------------------------------------------------------|--------------------------------------|
| 1    | CONSTRUCTION CERTIFICATE ISSUE | AA  | 01/07/2025 | THESE DRAWINGS ARE PRELIMINARY DRAWINGS AND ARE SUBJECT TO CHANGE WITHOUT NOTICE DURING THE COURSE OF THE PROPOSED DEVELOPMENT AND IN CONSULTATION WITH COUNCIL.<br>-DRAWINGS MADE TO A LARGER SCALE AND THOSE SHOWING PARTICULAR DETAIL OF WORKS SHALL TAKE PRECEDENCE OVER DRAWINGS MADE TO A SMALLER SCALE AND FOR MORE GENERAL PURPOSES<br>-WHERE ANY DISCREPANCY EXISTS BETWEEN FIGURED AND SCALED DIMENSIONS, THE FIGURED DIMENSIONS SHALL PREVAIL.<br>-BUILDER TO CHECK ALL SITE DIMENSIONS PRIOR TO FABRICATION OF FITMENTS<br>-BEFORE CARRYING OUT ANY WORK ENSURE THAT THE DRAWINGS USED CARRY THE LATEST AMENDMENT NO. | ARCHITECT<br><div>STUDIOHAUS</div> <div>E:CONNECT@STUDIOHAUS.COM.AU<br/>P:•61433571784</div> | COVER SHEET                          |
| 2    | CONSTRUCTION CERTIFICATE       | AA  | 25/11/2025 |   |                                                                                              | PROJECT NUMBER156DWG NUMBERA000      |
|      |                                |     |            |   |                                                                                              | SCALEREVISION2NORTH                  |
|      |                                |     |            | THESE DOCUMENTS AND ANY WORKS EXECUTED AS A RESULT OF THESE DOCUMENTS SHALL BE SUBJECT TO THE COPYRIGHT CONDITIONS SET OUT IN THE CONDITIONS OF ENGAGEMENT ©   |                                                                                              | PROJECTLOT 515                       |
|      |                                |     |            |   |                                                                                              | ADDRESSLOT 515, THORPE WAY, BOX HILL |








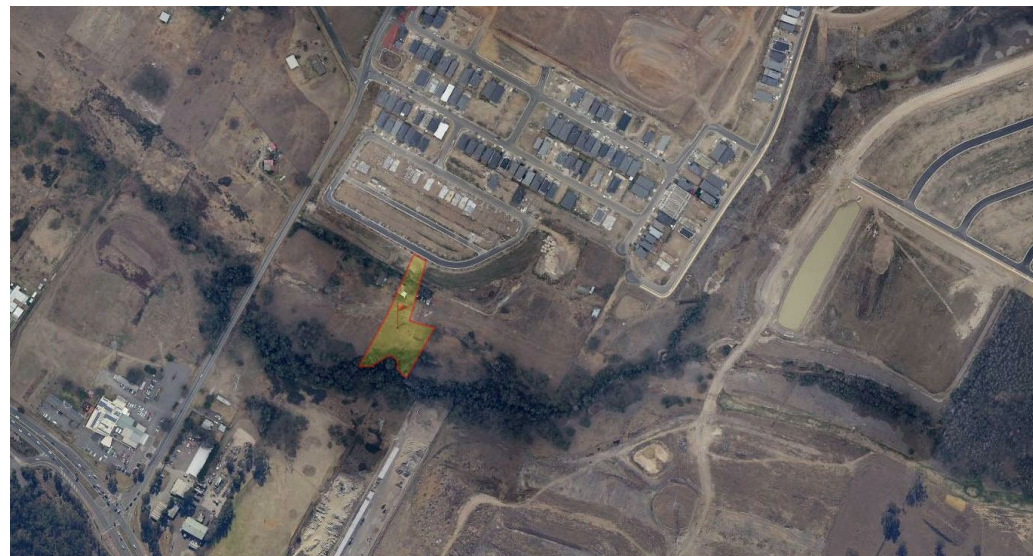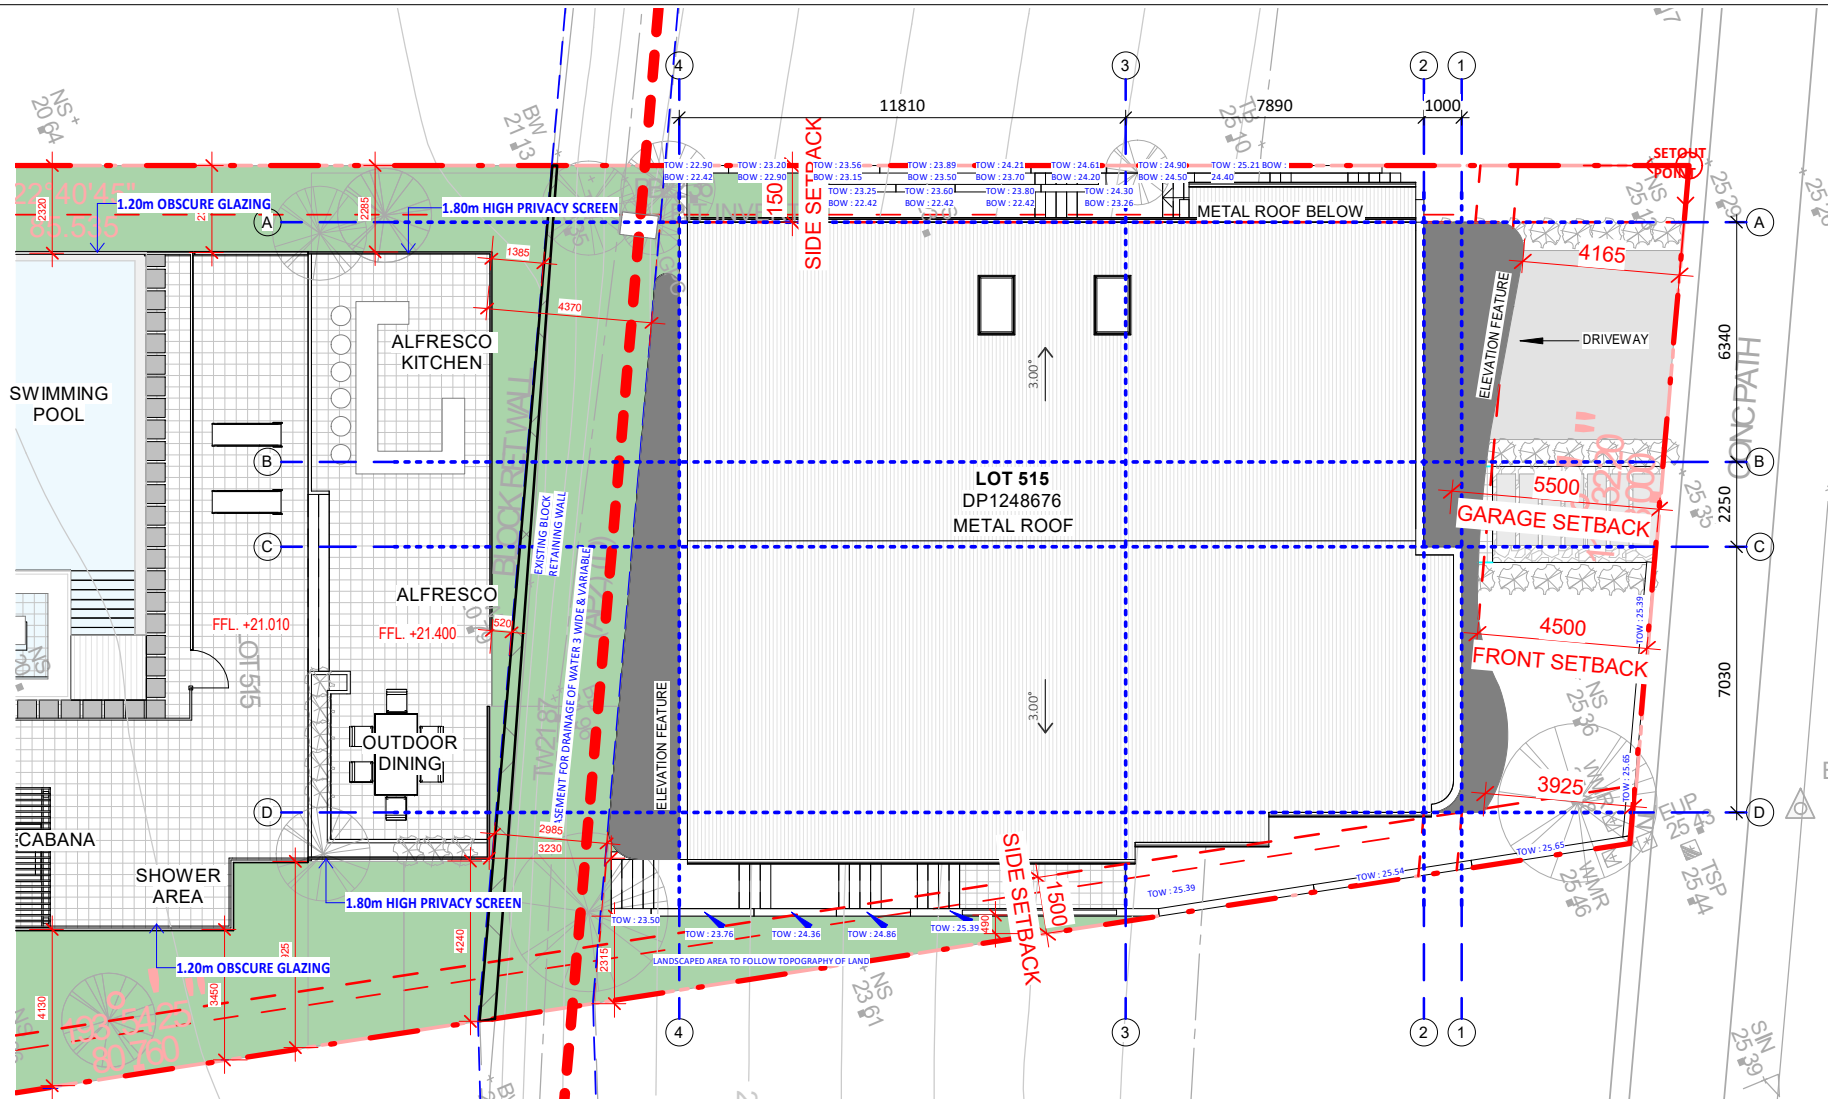


LOCATION PLAN

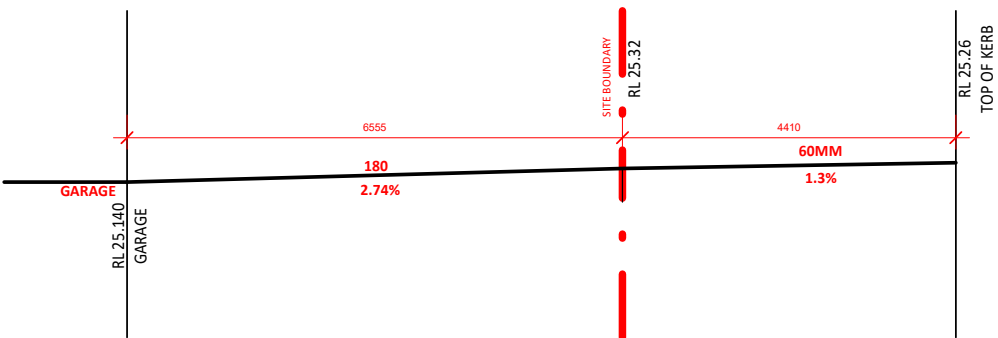

DRIVEWAY PROFILE

1 : 100

APPROX. ALIGNMENT OF EX-STORMWATER PIPE  
WITHIN EX-STORMWATER EASEMENT  
DETAILS (S.T.B.C.)

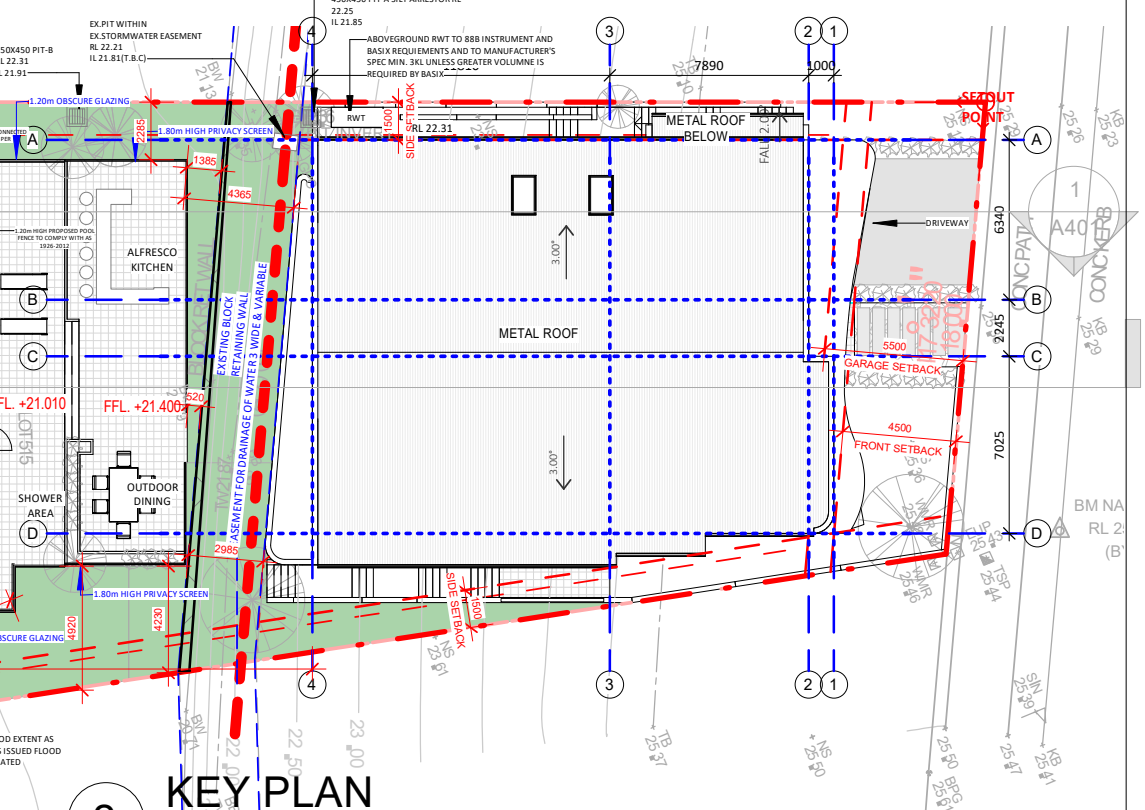

KEY PLAN

2  
1 : 300

| REV. | DESCRIPTION                    | BY. | DATE       |
|------|--------------------------------|-----|------------|
| 1    | CONSTRUCTION CERTIFICATE ISSUE | AA  | 01/07/2025 |
| 2    | CONSTRUCTION CERTIFICATE       | AA  | 25/11/2025 |


**NOTES**

- THESE DRAWINGS ARE PRELIMINARY DRAWINGS AND ARE SUBJECT TO CHANGE WITHOUT NOTICE DURING THE COURSE OF THE PROPOSED DEVELOPMENT AND IN CONSULTATION WITH COUNCIL.
- DRAWINGS MADE TO A LARGER SCALE AND THOSE SHOWING PARTICULAR DETAIL OF WORKS SHALL TAKE PRECEDENCE OVER DRAWINGS MADE TO A SMALLER SCALE AND FOR MORE GENERAL PURPOSES.
- WHERE ANY DISCREPANCY EXISTS BETWEEN FIGURED AND SCALED DIMENSIONS, THE FIGURED DIMENSIONS SHALL PREVAIL.
- BUILDER TO CHECK ALL SITE DIMENSIONS PRIOR TO FABRICATION OF FITMENTS.
- BEFORE CARRYING OUT ANY WORK ENSURE THAT THE DRAWINGS USED CARRY THE LATEST AMENDMENT NO.

THESE DOCUMENTS AND ANY WORKS EXECUTED AS A RESULT OF THESE DOCUMENTS SHALL BE SUBJECT TO THE COPYRIGHT CONDITIONS SET OUT IN THE CONDITIONS OF ENGAGEMENT ©

CLIENT  
ARCHITECT  
**STUDIOHAUS**  
E:CONNECT@STUDIOHAUS.COM.AU  
P: +61433571784

| DRAWING TITLE             |                               |            |      |
|---------------------------|-------------------------------|------------|------|
| LOCATION PLAN & SITE PLAN |                               |            |      |
| PROJECT NUMBER            | 156                           | DWG NUMBER | A100 |
| SCALE                     | AS INDICATED                  | REVISION   | 2    |
| PROJECT                   | LOT 515                       |            |      |
| ADDRESS                   | LOT 515, THORPE WAY, BOX HILL |            |      |

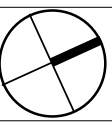






REFER TO DA COND 55 - PRIVACY SCREEN REQUIRED TO BE POSITIONED IN AN UPWARD POSITION TO AVOID DOWNWARD VIEW

GROUND STATIC WATER SUPPLY

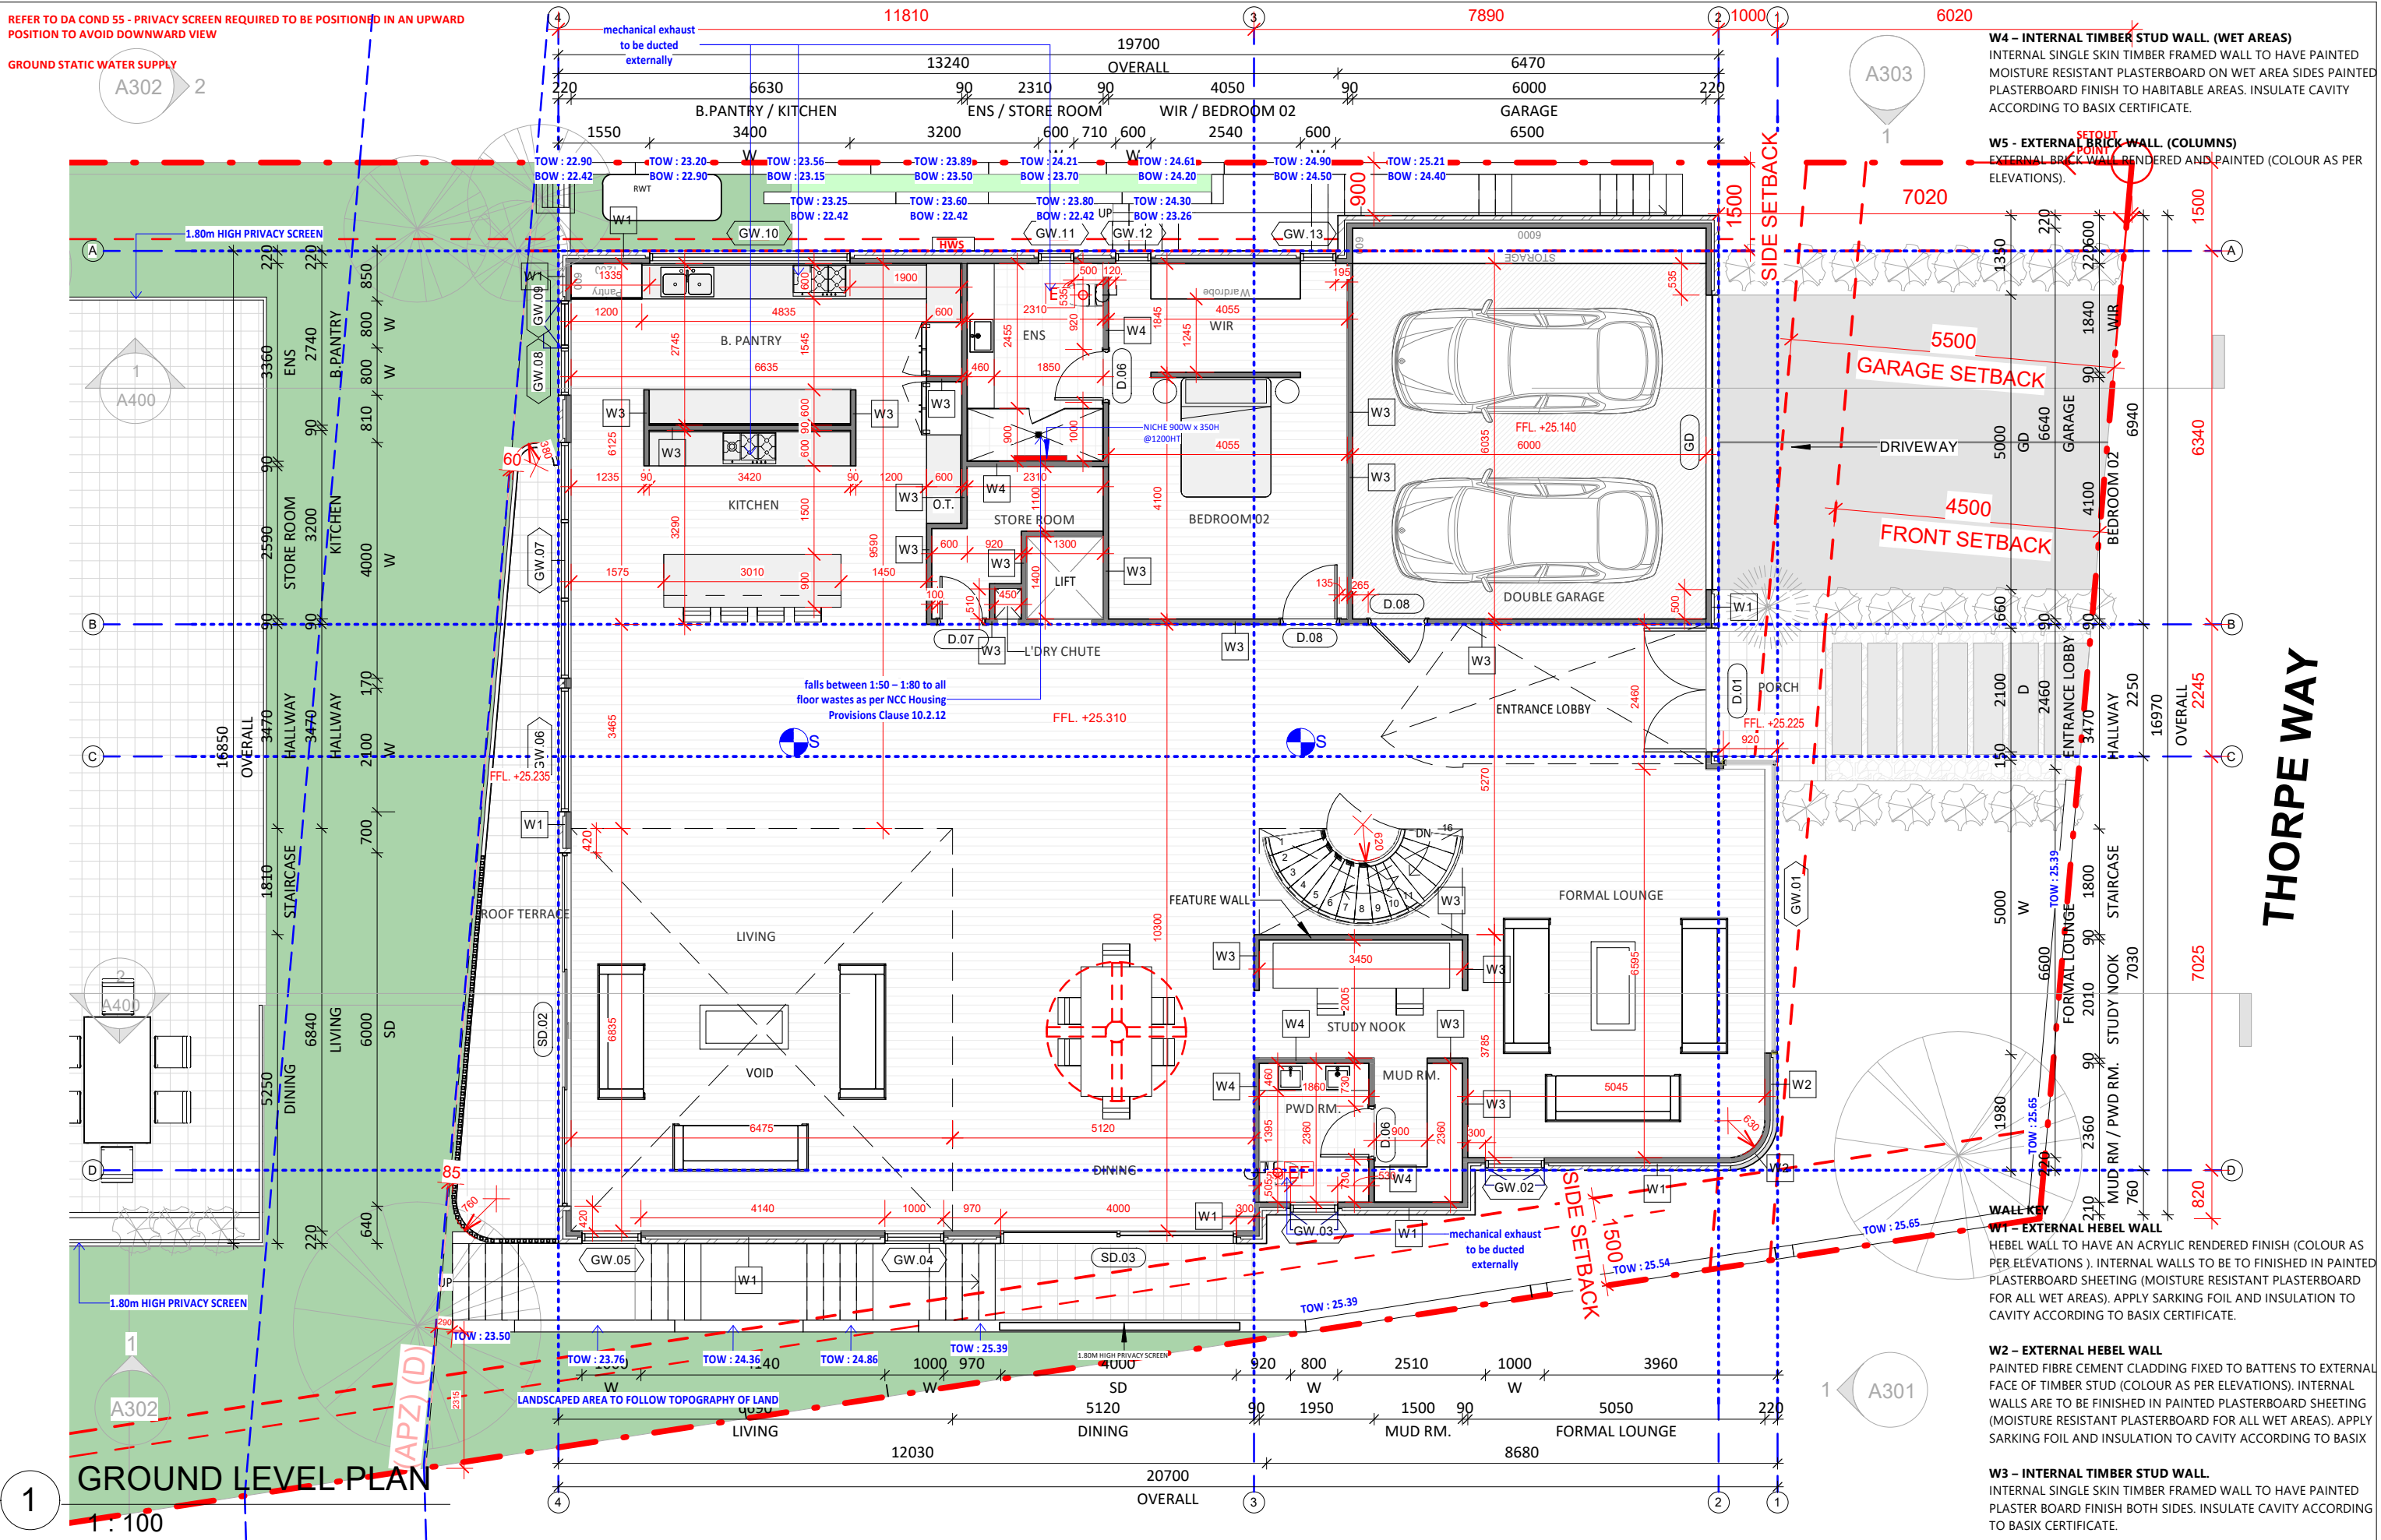

| REV. | DESCRIPTION                    | BY. | DATE       |
|------|--------------------------------|-----|------------|
| 1    | CONSTRUCTION CERTIFICATE ISSUE | AA  | 01/07/2025 |
| 2    | CONSTRUCTION CERTIFICATE       | AA  | 25/11/2025 |

**NOTES**

- THESE DRAWINGS ARE PRELIMINARY DRAWINGS AND ARE SUBJECT TO CHANGE WITHOUT NOTICE DURING THE COURSE OF THE PROPOSED DEVELOPMENT AND IN CONSULTATION WITH COUNCIL.

- DRAWINGS MADE TO A LARGER SCALE AND THOSE SHOWING PARTICULAR DETAIL OF WORKS SHALL TAKE PRECEDENCE OVER DRAWINGS MADE TO A SMALLER SCALE AND FOR MORE GENERAL PURPOSES.

- WHERE ANY DISCREPANCY EXISTS BETWEEN FIGURED AND SCALED DIMENSIONS, THE FIGURED DIMENSIONS SHALL PREVAIL.

- BUILDER TO CHECK ALL SITE DIMENSIONS PRIOR TO FABRICATION OF FITMENTS.

- BEFORE CARRYING OUT ANY WORK ENSURE THAT THE DRAWINGS USED CARRY THE LATEST AMENDMENT NO.

THESE DOCUMENTS AND ANY WORKS EXECUTED AS A RESULT OF THESE DOCUMENTS SHALL BE SUBJECT TO THE COPYRIGHT CONDITIONS SET OUT IN THE CONDITIONS OF ENGAGEMENT ©

CLIENT

ARCHITECT

**STUDIOHAUS**

E: CONNECT@STUDIOHAUS.COM.AU  
P: +61433571784

| DRAWING TITLE     |                               |            |      |
|-------------------|-------------------------------|------------|------|
| GROUND FLOOR PLAN |                               |            |      |
| PROJECT NUMBER    | 156                           | DWG NUMBER | A201 |
| SCALE             | 1:100                         | REVISION   | 2    |
| PROJECT           | LOT 515                       | NORTH      |      |
| ADDRESS           | LOT 515, THORPE WAY, BOX HILL |            |      |

THORPE WAY

REFER TO DA COND 55 - PRIVACY SCREEN REQUIRED TO BE POSITIONED IN AN UPWARD POSITION TO AVOID DOWNWARD VIEW

GROUND STATIC WATER SUPPLY

W4 - INTERNAL TIMBER STUD WALL. (WET AREAS)

INTERNAL SINGLE SKIN TIMBER FRAMED WALL TO HAVE PAINTED MOISTURE RESISTANT PLASTERBOARD ON WET AREA SIDES PAINTED PLASTERBOARD FINISH TO HABITABLE AREAS. INSULATE CAVITY ACCORDING TO BASIX CERTIFICATE.

W5 - EXTERNAL BRICK WALL. (COLUMNS)

EXTERNAL BRICK WALL RENDERED AND PAINTED (COLOUR AS PER ELEVATIONS).

WALL KEY

W1 - EXTERNAL HEBEL WALL  
HEBEL WALL TO HAVE AN ACRYLIC RENDERED FINISH (COLOUR AS PER ELEVATIONS). INTERNAL WALLS TO BE TO FINISHED IN PAINTED PLASTERBOARD SHEETING (MOISTURE RESISTANT PLASTERBOARD FOR ALL WET AREAS). APPLY SARKING FOIL AND INSULATION TO CAVITY ACCORDING TO BASIX CERTIFICATE.

W2 - EXTERNAL HEBEL WALL

PAINTED FIBRE CEMENT CLADDING FIXED TO BATTENS TO EXTERNAL FACE OF TIMBER STUD (COLOUR AS PER ELEVATIONS). INTERNAL WALLS ARE TO BE FINISHED IN PAINTED PLASTERBOARD SHEETING (MOISTURE RESISTANT PLASTERBOARD FOR ALL WET AREAS). APPLY SARKING FOIL AND INSULATION TO CAVITY ACCORDING TO BASIX

W3 - INTERNAL TIMBER STUD WALL.

INTERNAL SINGLE SKIN TIMBER FRAMED WALL TO HAVE PAINTED PLASTER BOARD FINISH BOTH SIDES. INSULATE CAVITY ACCORDING TO BASIX CERTIFICATE.

# FIRST LEVEL PLAN

1 : 100

| REV. | DESCRIPTION                    | BY. | DATE       |
|------|--------------------------------|-----|------------|
| 1    | CONSTRUCTION CERTIFICATE ISSUE | AA  | 01/07/2025 |
| 2    | CONSTRUCTION CERTIFICATE       | AA  | 25/11/2025 |
|      |                                |     |            |
|      |                                |     |            |
|      |                                |     |            |

NOTES  
-THESE DRAWINGS ARE PRELIMINARY DRAWINGS AND ARE SUBJECT TO CHANGE WITHOUT NOTICE DURING THE COURSE OF THE PROPOSED DEVELOPMENT AND IN CONSULTATION WITH COUNCIL.  
-DRAWINGS MADE TO A LARGER SCALE AND THOSE SHOWING PARTICULAR DETAIL OF WORKS SHALL TAKE PRECEDENCE OVER DRAWINGS MADE TO A SMALLER SCALE AND FOR MORE GENERAL PURPOSES  
-WHERE ANY DISCREPANCY EXISTS BETWEEN FIGURED AND SCALED DIMENSIONS, THE FIGURED DIMENSIONS SHALL PREVAIL.  
-BUILDER TO CHECK ALL SITE DIMENSIONS PRIOR TO FABRICATION OF FITMENTS  
-BEFORE CARRYING OUT ANY WORK ENSURE THAT THE DRAWINGS USED CARRY THE LATEST AMENDMENT NO.

THESE DOCUMENTS AND ANY WORKS EXECUTED AS A RESULT OF THESE DOCUMENTS SHALL BE SUBJECT TO THE COPYRIGHT CONDITIONS SET OUT IN THE CONDITIONS OF ENGAGEMENT ©


CLIENT  
ARCHITECT  
**STUDIOHAUS**  
E:CONNECT@STUDIOHAUS.COM.AU  
P: +61433571784

|                |        |                               |      |
|----------------|--------|-------------------------------|------|
| DRAWING TITLE  |        | FIRST FLOOR PLAN              |      |
| PROJECT NUMBER | 156    | DWG NUMBER                    | A202 |
| SCALE          | 1: 100 | REVISION                      | 2    |
| PROJECT        |        | LOT 515                       |      |
| ADDRESS        |        | LOT 515, THORPE WAY, BOX HILL |      |








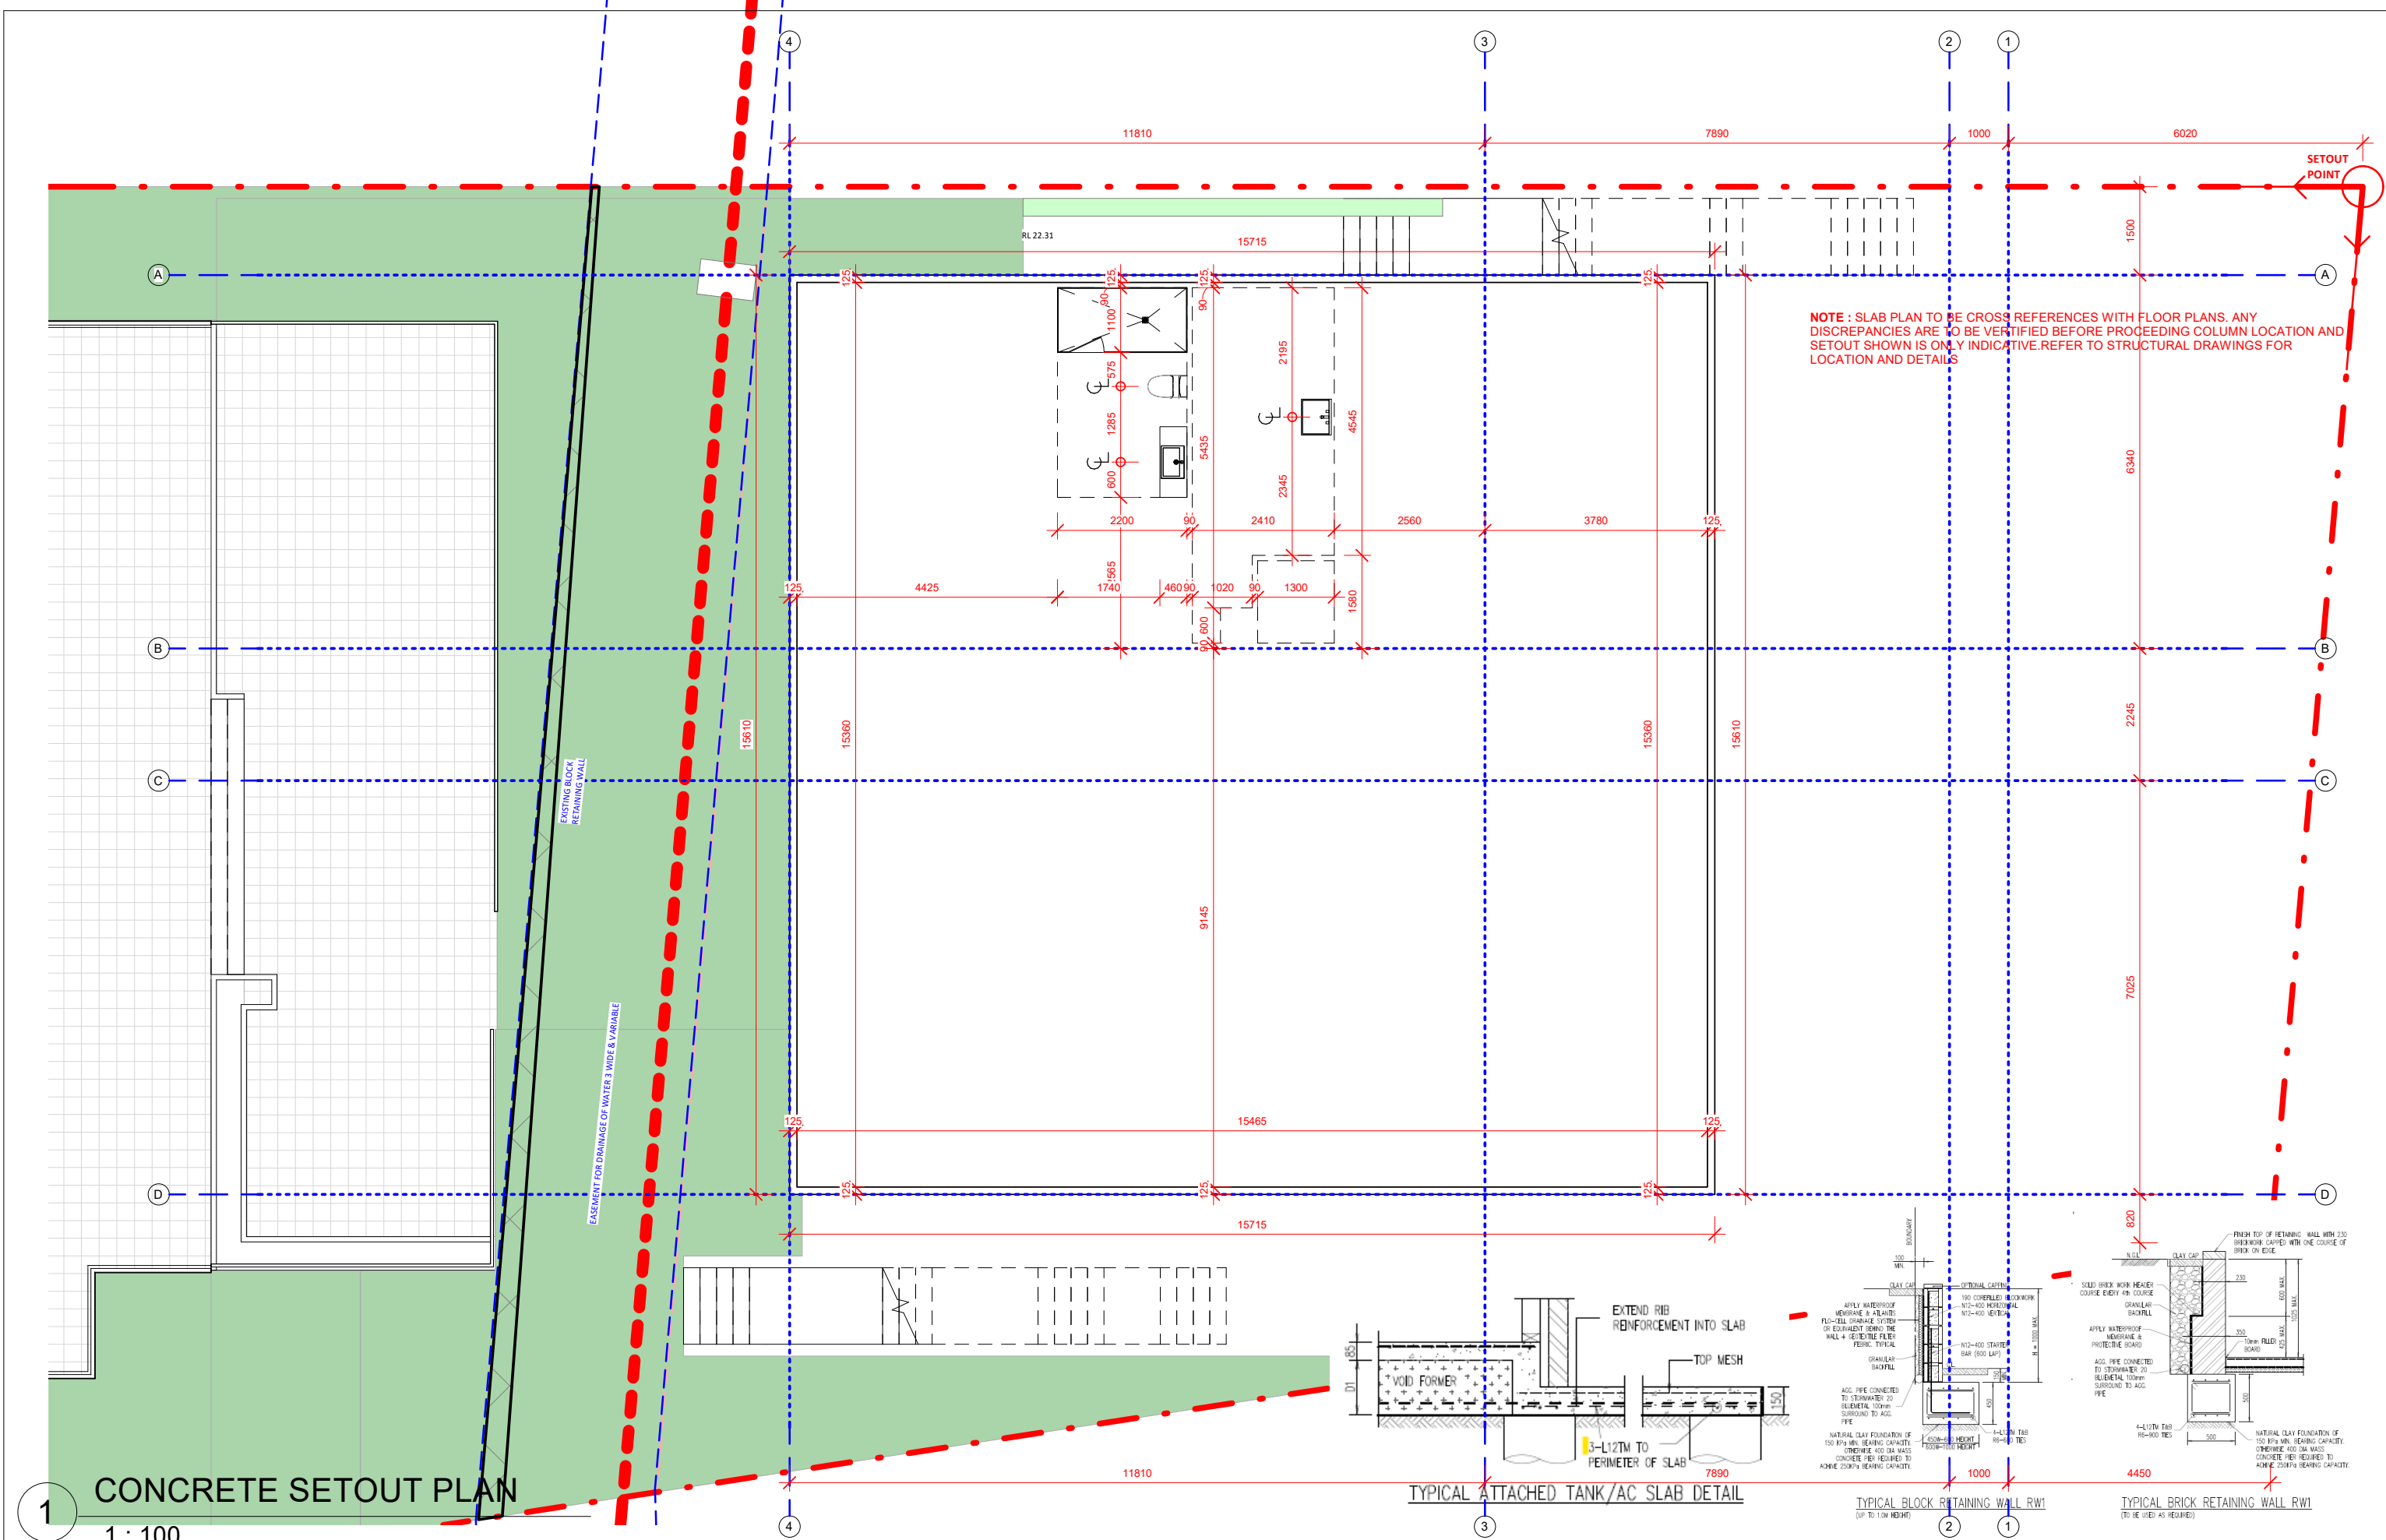


| |
|---|
| |
|---|



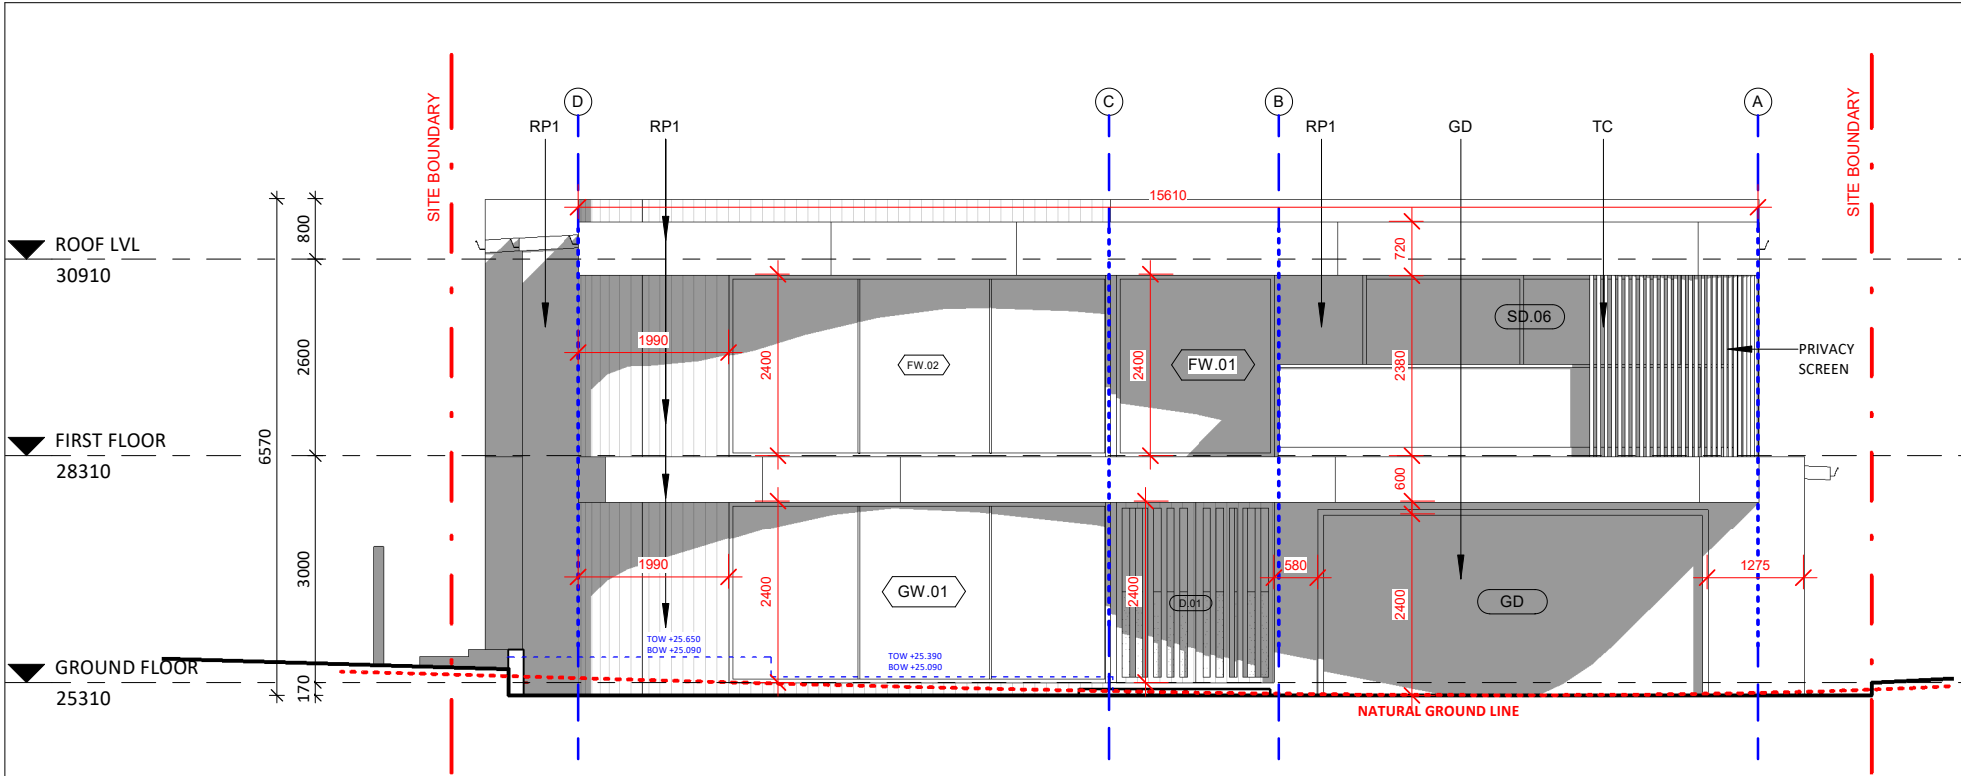

1 NORTH EAST ELEVATION  
1 : 100

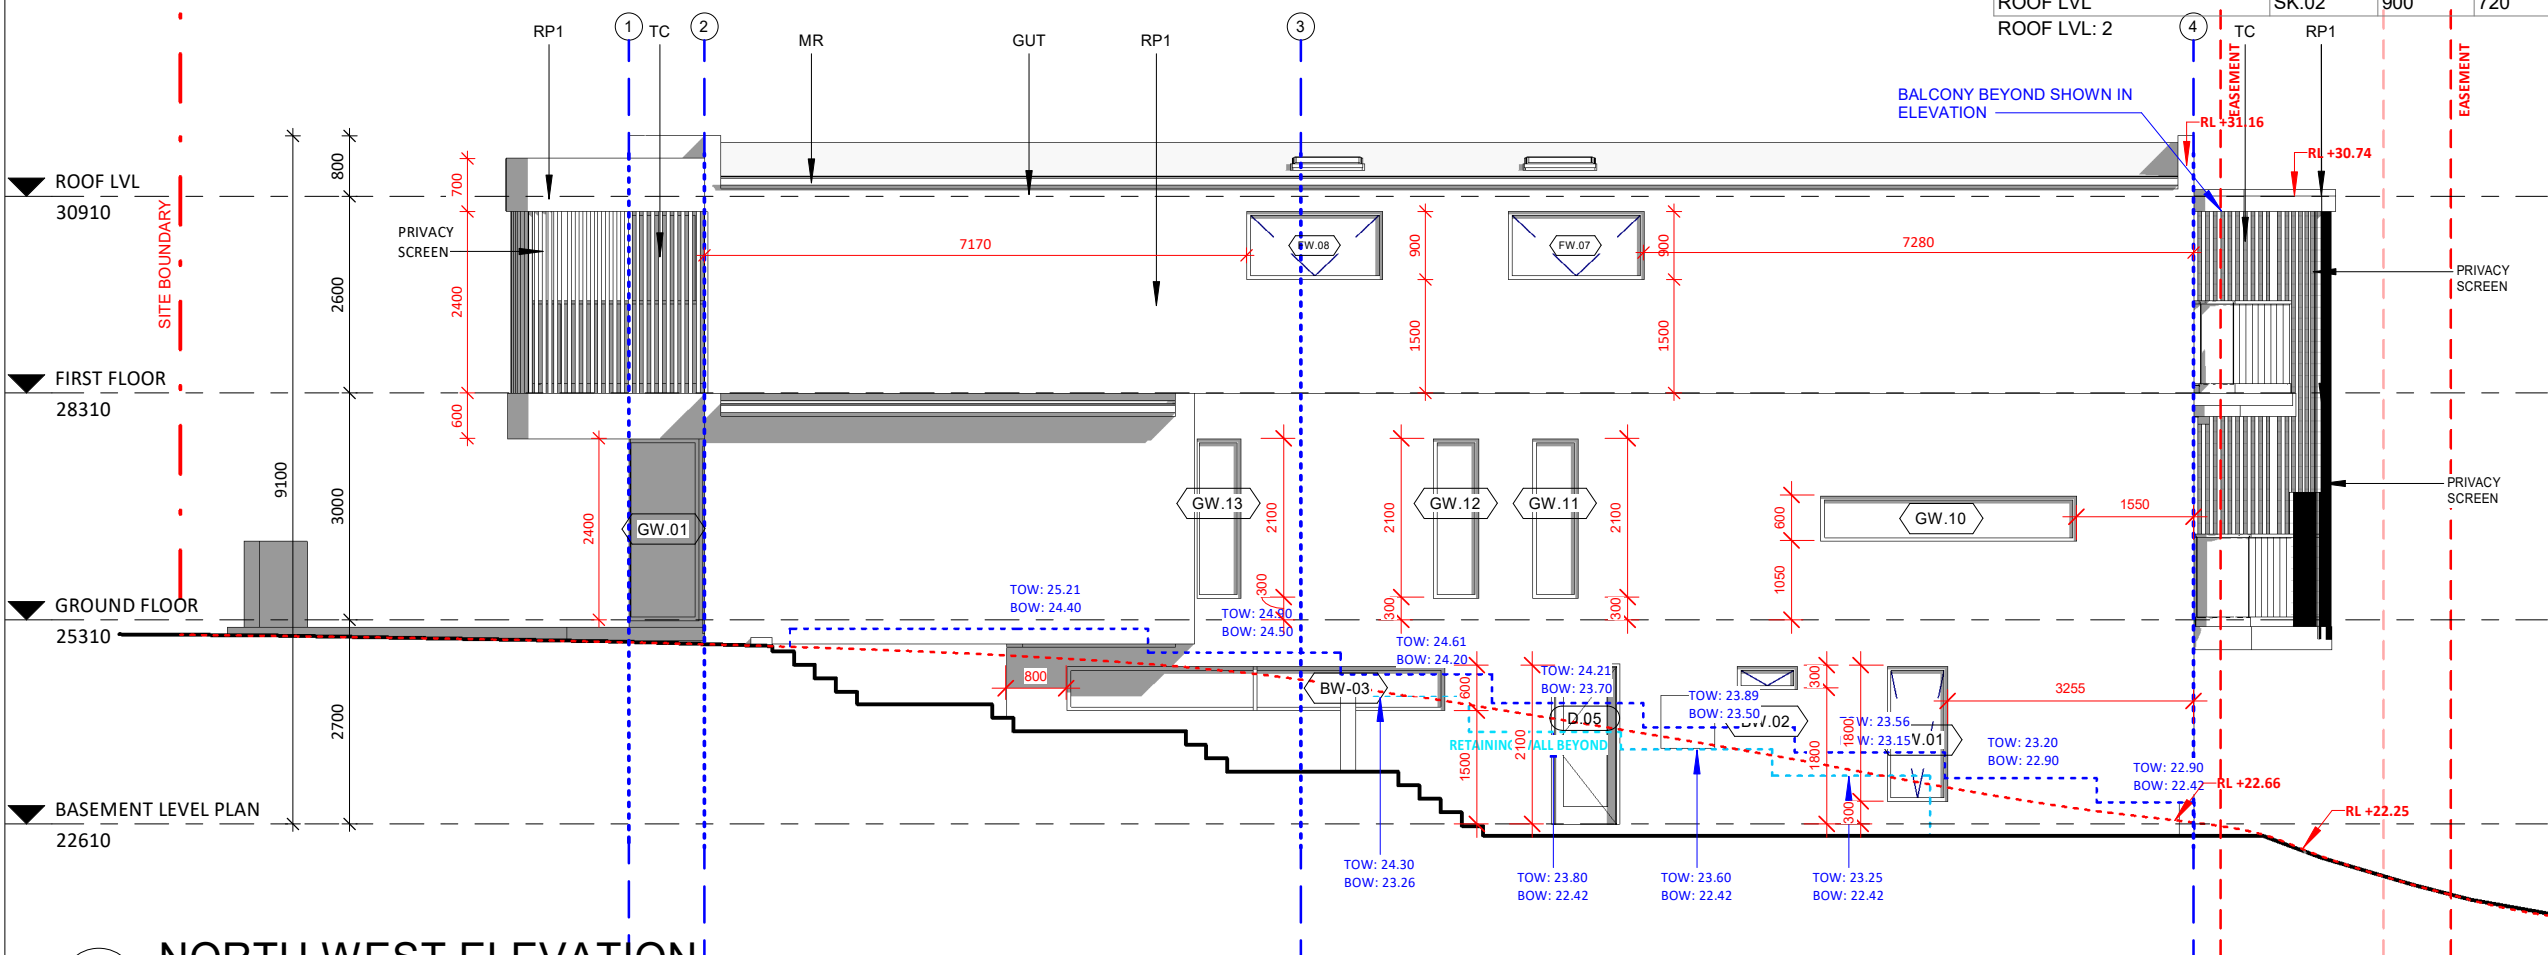

2 NORTH WEST ELEVATION  
1 : 100

| WINDOW OPENING SCHEDULE |       |          |        |             |             |                     |
|-------------------------|-------|----------|--------|-------------|-------------|---------------------|
| LEVEL                   | MARK  | WIDTH    | HEIGHT | SILL HEIGHT | HEAD HEIGHT | COMMENTS            |
| BASEMENT LEVEL PLAN     | BW.01 | 800      | 1800   | 300         | 2100        | AWNING              |
| BASEMENT LEVEL PLAN     | BW.02 | 800      | 300    | 1800        | 2100        | AWNING              |
| BASEMENT LEVEL PLAN     | BW.03 | 5000     | 600    | 1500        | 2100        | SLIDING             |
| BASEMENT LEVEL PLAN     | BW.04 | 3500     | 1800   | 300         | 2100        | SLIDING             |
| BASEMENT LEVEL PLAN     | BW.05 | 2000     | 600    | 1500        | 2100        | SLIDING             |
| BASEMENT LEVEL PLAN: 5  |       |          |        |             |             |                     |
| GROUND FLOOR            | GW.01 | 5000/900 | 2400   | 0           | 2400        | FIXED/CORNER        |
| GROUND FLOOR            | GW.02 | 1000     | 2100   | 300         | 2400        | AWNING              |
| GROUND FLOOR            | GW.03 | 800      | 2100   | 300         | 2400        | AWNING              |
| GROUND FLOOR            | GW.04 | 1000     | 2100   | 300         | 2400        | FIXED               |
| GROUND FLOOR            | GW.05 | 1000     | 2100   | 300         | 2400        | FIXED               |
| GROUND FLOOR            | GW.06 | 2100     | 2400   | 0           | 2400        | FIXED               |
| GROUND FLOOR            | GW.07 | 4000     | 2400   | 0           | 2400        | FIXED               |
| GROUND FLOOR            | GW.08 | 800      | 2400   | 0           | 2400        | FIXED               |
| GROUND FLOOR            | GW.09 | 800      | 2400   | 0           | 2400        | AWNING              |
| GROUND FLOOR            | GW.10 | 3400     | 600    | 1050        | 1650        | FIXED               |
| GROUND FLOOR            | GW.11 | 600      | 2100   | 300         | 2400        | AWNING              |
| GROUND FLOOR            | GW.12 | 600      | 2100   | 300         | 2400        | AWNING              |
| GROUND FLOOR            | GW.13 | 600      | 2100   | 300         | 2400        | AWNING              |
| GROUND FLOOR: 13        |       |          |        |             |             |                     |
| FIRST FLOOR             | FW.01 | 1650     | 2400   | 0           | 2400        | FIXED               |
| FIRST FLOOR             | FW.02 | 5000/900 | 2400   | 0           | 2400        | FIXED/AWNING/CORNER |
| FIRST FLOOR             | FW.03 | 750      | 600    | 1800        | 2400        | AWNING              |
| FIRST FLOOR             | FW.04 | 3000     | 700    | 1700        | 2400        | SLIDING             |
| FIRST FLOOR             | FW.05 | 5100     | 2400   | 0           | 2400        | FIXED               |
| FIRST FLOOR             | FW.06 | 6000     | 2400   | 0           | 2400        | FIXED               |
| FIRST FLOOR             | FW.07 | 1800     | 900    | 1500        | 2400        | AWNING              |
| FIRST FLOOR             | FW.08 | 1800     | 900    | 1500        | 2400        | AWNING              |
| FIRST FLOOR: 8          |       |          |        |             |             |                     |
| ROOF LVL                | SK.01 | 900      | 720    |             |             | SKYLIGHT            |
| ROOF LVL                | SK.02 | 900      | 720    |             |             | SKYLIGHT            |
| ROOF LVL: 2             |       |          |        |             |             |                     |

| ELEVATION LEGEND |                       |
|------------------|-----------------------|
| FB               | FACE BRICK            |
| RP1/RP2/RP3      | RENDERED & PAINTED    |
| WC1/WC2          | LIGHT WEIGHT CLADDING |
| CRT              | CONCRETE ROOF TILE    |
| TD               | TIMBER DOOR           |
| SD               | SLIDING DOOR          |
| GD               | GARAGE DOOR           |
| DP               | DOWN PIPE             |
| FAS              | FASCIA                |
| GUT              | GUTTER                |
| HWS              | HOT WATER SYSTEM      |
| RWT              | RAIN WATER TANK       |
| AC               | AIR CONDITIONING UNIT |
| GM               | GAS METER             |
| EM               | ELECTRICITY METER     |
| W                | WINDOW FRAME          |
| MR               | METAL ROOF            |
| SL               | SKYLIGHT              |


| MATERIAL LEGEND |             |
|-----------------|-------------|
| RP1             | LEXICON QTR |
| TC              | BAMBOO LOOK |
| MR              | WINDSPRAY   |
| GD              | GARAGE DOOR |
| W               | MONUMENT    |

| REV. | DESCRIPTION                    | BY. | DATE       |
|------|--------------------------------|-----|------------|
| 1    | CONSTRUCTION CERTIFICATE ISSUE | AA  | 01/07/2025 |
| 2    | CONSTRUCTION CERTIFICATE       | AA  | 25/11/2025 |


**NOTES**  
-THESE DRAWINGS ARE PRELIMINARY DRAWINGS AND ARE SUBJECT TO CHANGE WITHOUT NOTICE DURING THE COURSE OF THE PROPOSED DEVELOPMENT AND IN CONSULTATION WITH COUNCIL.  
-DRAWINGS MADE TO A LARGER SCALE AND THOSE SHOWING PARTICULAR DETAIL OF WORKS SHALL TAKE PRECEDENCE OVER DRAWINGS MADE TO A SMALLER SCALE AND FOR MORE GENERAL PURPOSES  
-WHERE ANY DISCREPANCY EXISTS BETWEEN FIGURED AND SCALED DIMENSIONS, THE FIGURED DIMENSIONS SHALL PREVAIL.  
-BUILDER TO CHECK ALL SITE DIMENSIONS PRIOR TO FABRICATION OF FITMENTS  
-BEFORE CARRYING OUT ANY WORK ENSURE THAT THE DRAWINGS USED CARRY THE LATEST AMENDMENT NO.

THESE DOCUMENTS AND ANY WORKS EXECUTED AS A RESULT OF THESE DOCUMENTS SHALL BE SUBJECT TO THE COPYRIGHT CONDITIONS SET OUT IN THE CONDITIONS OF ENGAGEMENT ©

| CLIENT                                         |  | DRAWING TITLE                         |  | PROPOSED ELEVATIONS |  |
|------------------------------------------------|--|---------------------------------------|--|---------------------|--|
| ARCHITECT                                      |  | PROJECT NUMBER 156                    |  | DWG NUMBER A301     |  |
| STUDIOHAUS                                     |  | SCALE AS INDICATED                    |  | REVISION 2 NORTH    |  |
| E:CONNECT@STUDIOHAUS.COM.AU<br>P: +61433571784 |  | PROJECT LOT 515                       |  |                     |  |
|                                                |  | ADDRESS LOT 515, THORPE WAY, BOX HILL |  |                     |  |

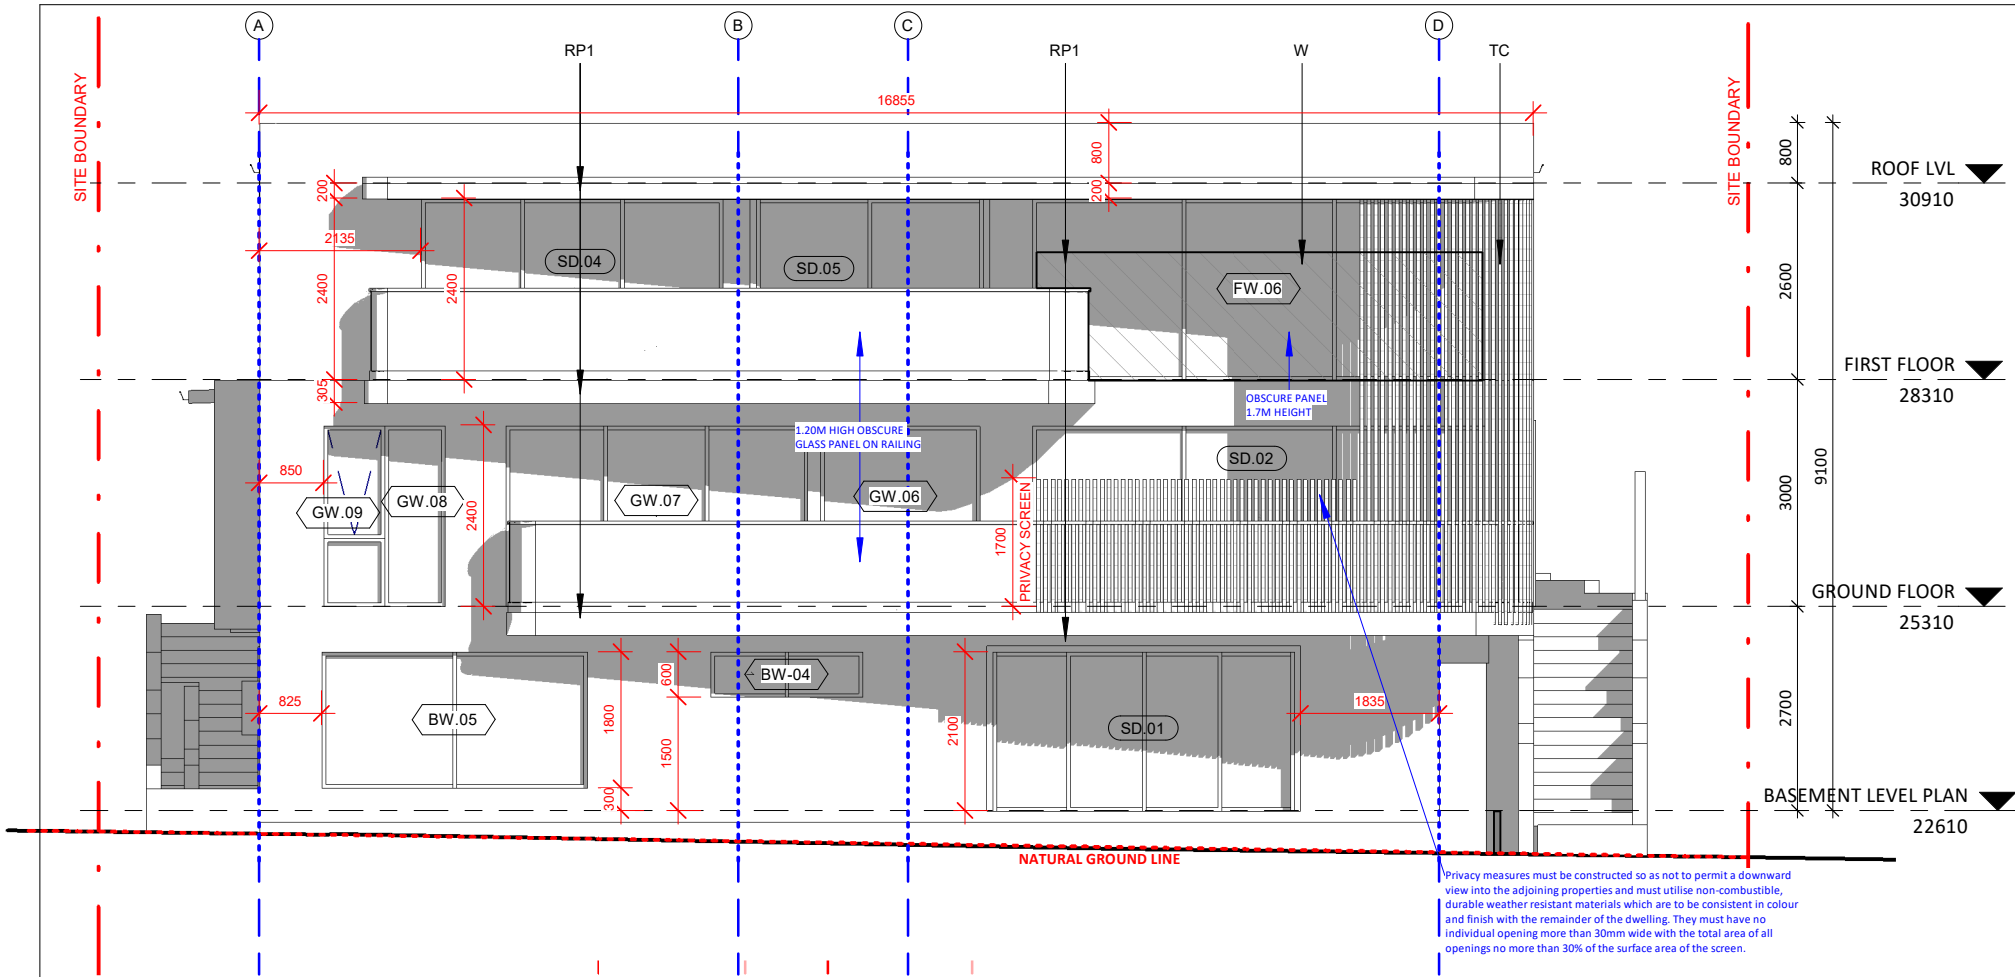

2 SOUTH WEST ELEVATION  
1 : 100

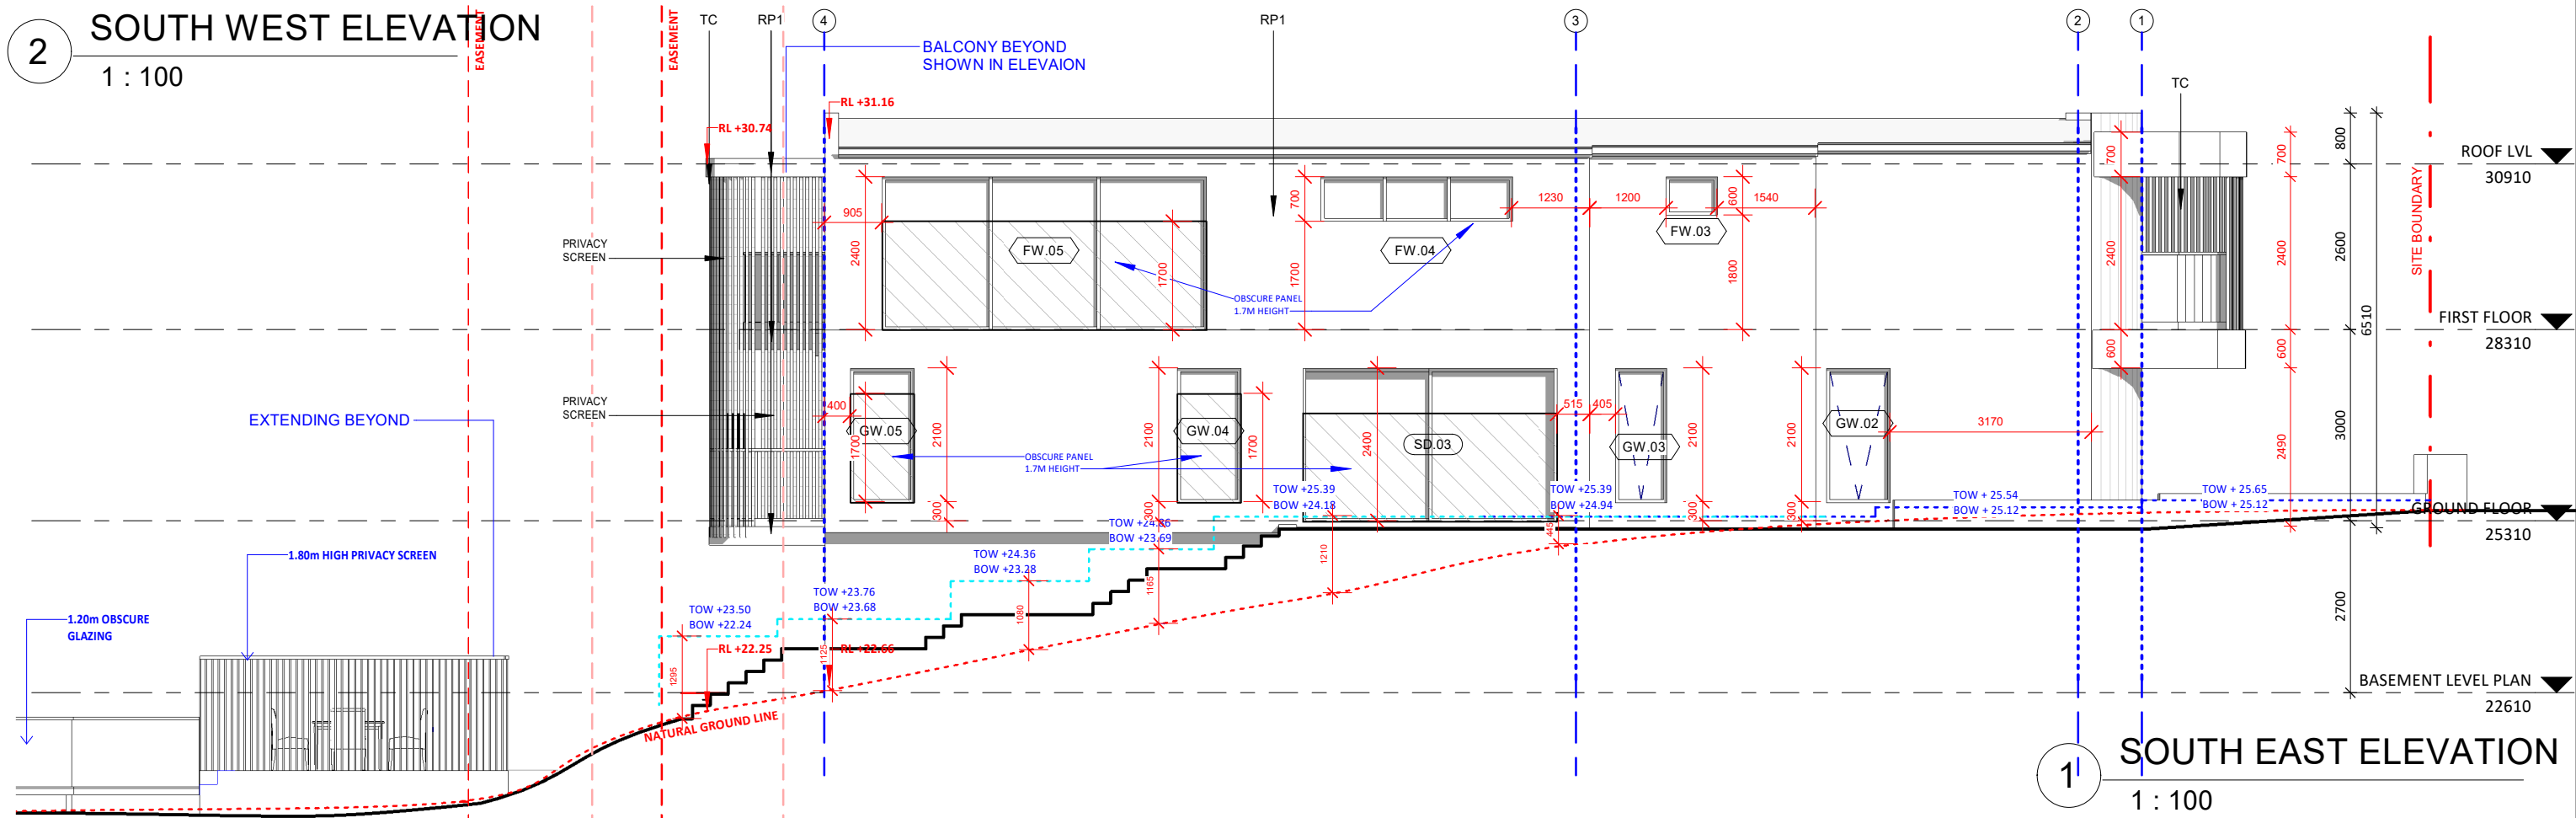

1 SOUTH EAST ELEVATION  
1 : 100

| REV. | DESCRIPTION                    | BY. | DATE       |
|------|--------------------------------|-----|------------|
| 1    | CONSTRUCTION CERTIFICATE ISSUE | AA  | 01/07/2025 |
| 2    | CONSTRUCTION CERTIFICATE       | AA  | 25/11/2025 |
|      |                                |     |            |
|      |                                |     |            |
|      |                                |     |            |

**NOTES**


- THESE DRAWINGS ARE PRELIMINARY DRAWINGS AND ARE SUBJECT TO CHANGE WITHOUT NOTICE DURING THE COURSE OF THE PROPOSED DEVELOPMENT AND IN CONSULTATION WITH COUNCIL.
- DRAWINGS MADE TO A LARGER SCALE AND THOSE SHOWING PARTICULAR DETAIL OF WORKS SHALL TAKE PRECEDENCE OVER DRAWINGS MADE TO A SMALLER SCALE AND FOR MORE GENERAL PURPOSES.
- WHERE ANY DISCREPANCY EXISTS BETWEEN FIGURED AND SCALED DIMENSIONS, THE FIGURED DIMENSIONS SHALL PREVAIL.
- BUILDER TO CHECK ALL SITE DIMENSIONS PRIOR TO FABRICATION OF FITMENTS.
- BEFORE CARRYING OUT ANY WORK ENSURE THAT THE DRAWINGS USED CARRY THE LATEST AMENDMENT NO.

THESE DOCUMENTS AND ANY WORKS EXECUTED AS A RESULT OF THESE DOCUMENTS SHALL BE SUBJECT TO THE COPYRIGHT CONDITIONS SET OUT IN THE CONDITIONS OF ENGAGEMENT ©


CLIENT  
ARCHITECT  
**STUDIOHAUS**  
E:CONNECT@STUDIOHAUS.COM.AU  
P:61433571784

| DRAWING TITLE  |                               |            |      | PROPOSED ELEVATIONS |  |
|----------------|-------------------------------|------------|------|---------------------|--|
| PROJECT NUMBER | 156                           | DWG NUMBER | A302 | NORTH               |  |
| SCALE          | 1 : 100                       | REVISION   | 2    |                     |  |
| PROJECT        | LOT 515                       |            |      |                     |  |
| ADDRESS        | LOT 515, THORPE WAY, BOX HILL |            |      |                     |  |




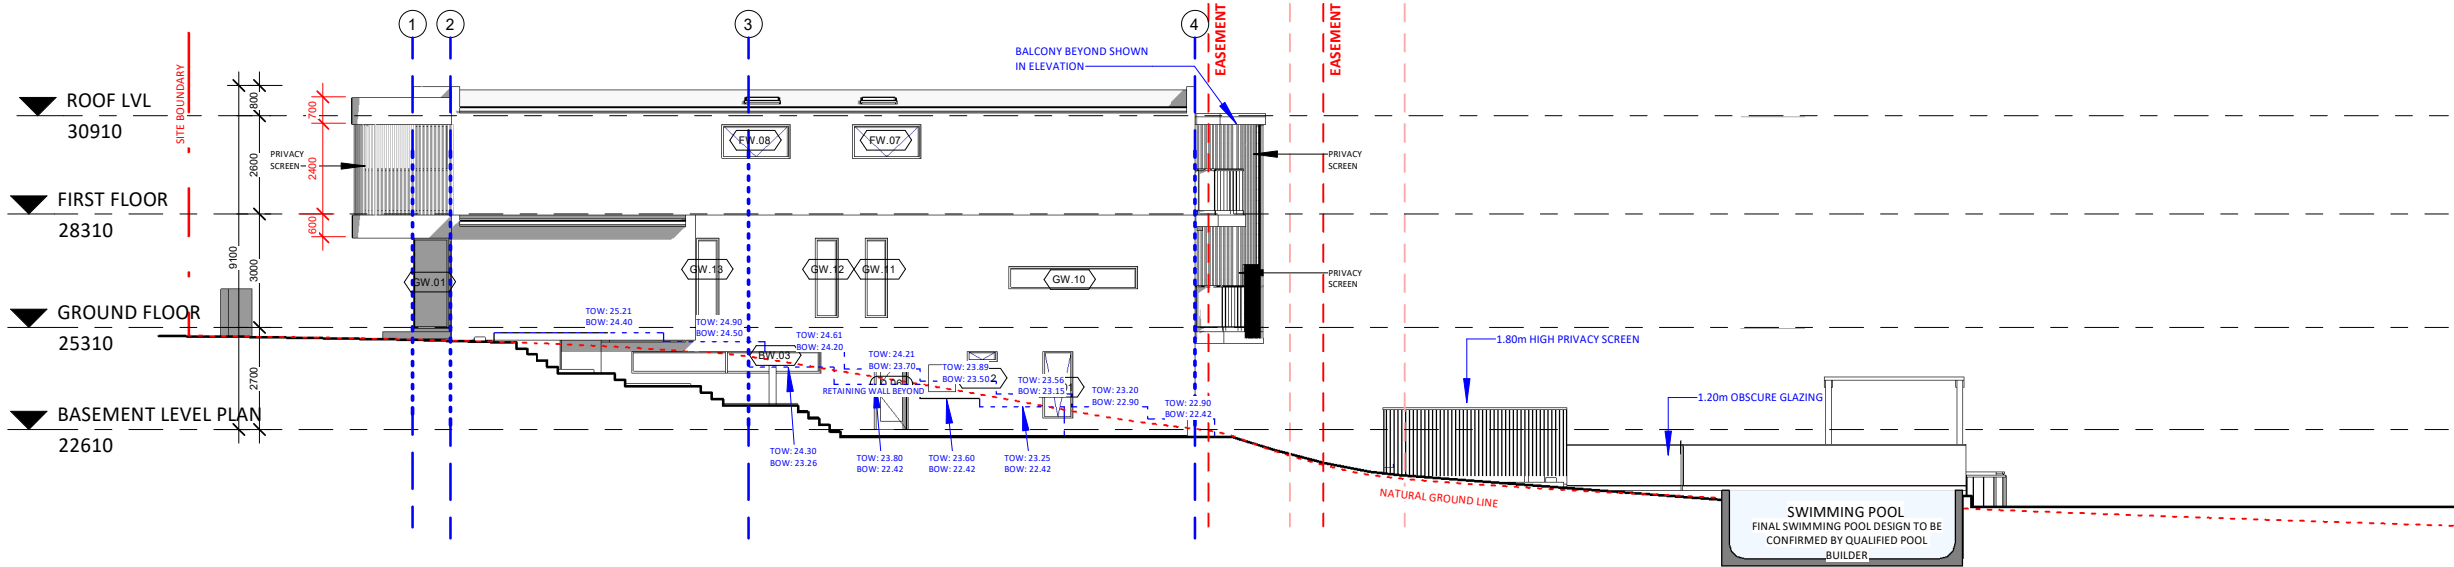


1 SITE ELEVATION - NORTH EAST ELEVATION  
1 : 200

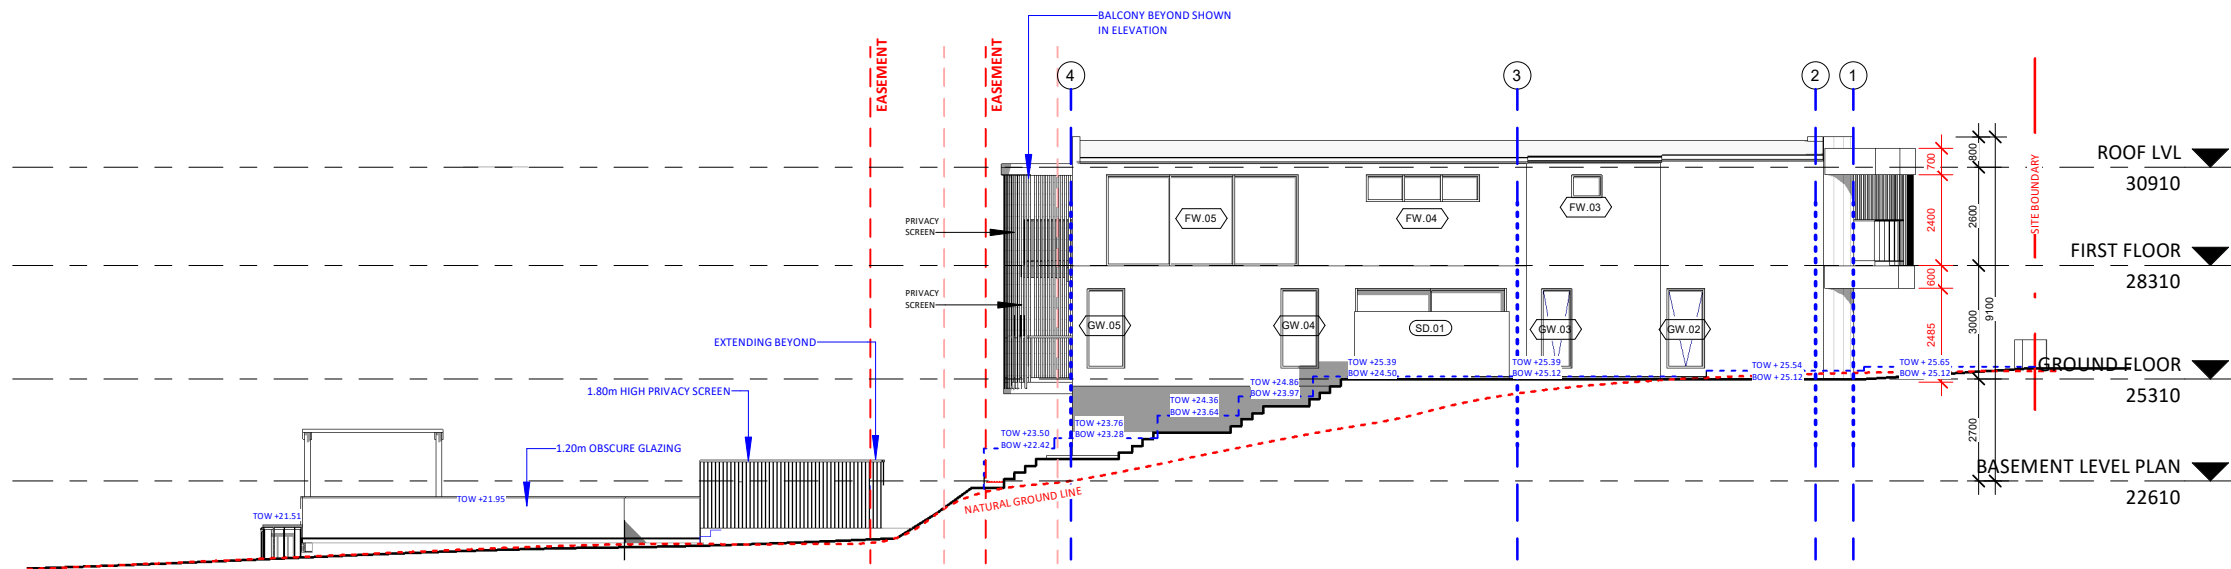

2 SITE ELEVATION - SOUTH WEST ELEVATION  
1 : 200

| REV. | DESCRIPTION                    | BY. | DATE       | NOTES   | CLIENT                                                                            | DRAWING TITLE                                                                                 |
|------|--------------------------------|-----|------------|---|-----------------------------------------------------------------------------------|-----------------------------------------------------------------------------------------------|
| 1    | CONSTRUCTION CERTIFICATE ISSUE | AA  | 01/07/2025 | THESE DRAWINGS ARE PRELIMINARY DRAWINGS AND ARE SUBJECT TO CHANGE WITHOUT NOTICE DURING THE COURSE OF THE PROPOSED DEVELOPMENT AND IN CONSULTATION WITH COUNCIL.<br>-DRAWINGS MADE TO A LARGER SCALE AND THOSE SHOWING PARTICULAR DETAIL OF WORKS SHALL TAKE PRECEDENCE OVER DRAWINGS MADE TO A SMALLER SCALE AND FOR MORE GENERAL PURPOSES<br>-WHERE ANY DISCREPANCY EXISTS BETWEEN FIGURED AND SCALED DIMENSIONS, THE FIGURED DIMENSIONS SHALL PREVAIL.<br>-BUILDER TO CHECK ALL SITE DIMENSIONS PRIOR TO FABRICATION OF FITMENTS<br>-BEFORE CARRYING OUT ANY WORK ENSURE THAT THE DRAWINGS USED CARRY THE LATEST AMENDMENT NO. | ARCHITECT<br><b>STUDIO</b> HAUS<br>E:CONNECT@STUDIOHAUS.COM.AU<br>P: +61433571784 | PROPOSED SITE ELEVATIONS                                                                      |
| 2    | CONSTRUCTION CERTIFICATE       | AA  | 25/11/2025 |   |                                                                                   | PROJECT NUMBER 156<br>SCALE 1:200<br>PROJECT LOT 515<br>ADDRESS LOT 515, THORPE WAY, BOX HILL |
|      |                                |     |            | THESE DOCUMENTS AND ANY WORKS EXECUTED AS A RESULT OF THESE DOCUMENTS SHALL BE SUBJECT TO THE COPYRIGHT CONDITIONS SET OUT IN THE CONDITIONS OF ENGAGEMENT ©   |                                                                                   | DWG NUMBER A303<br>REVISION 2<br>NORTH                                                        |

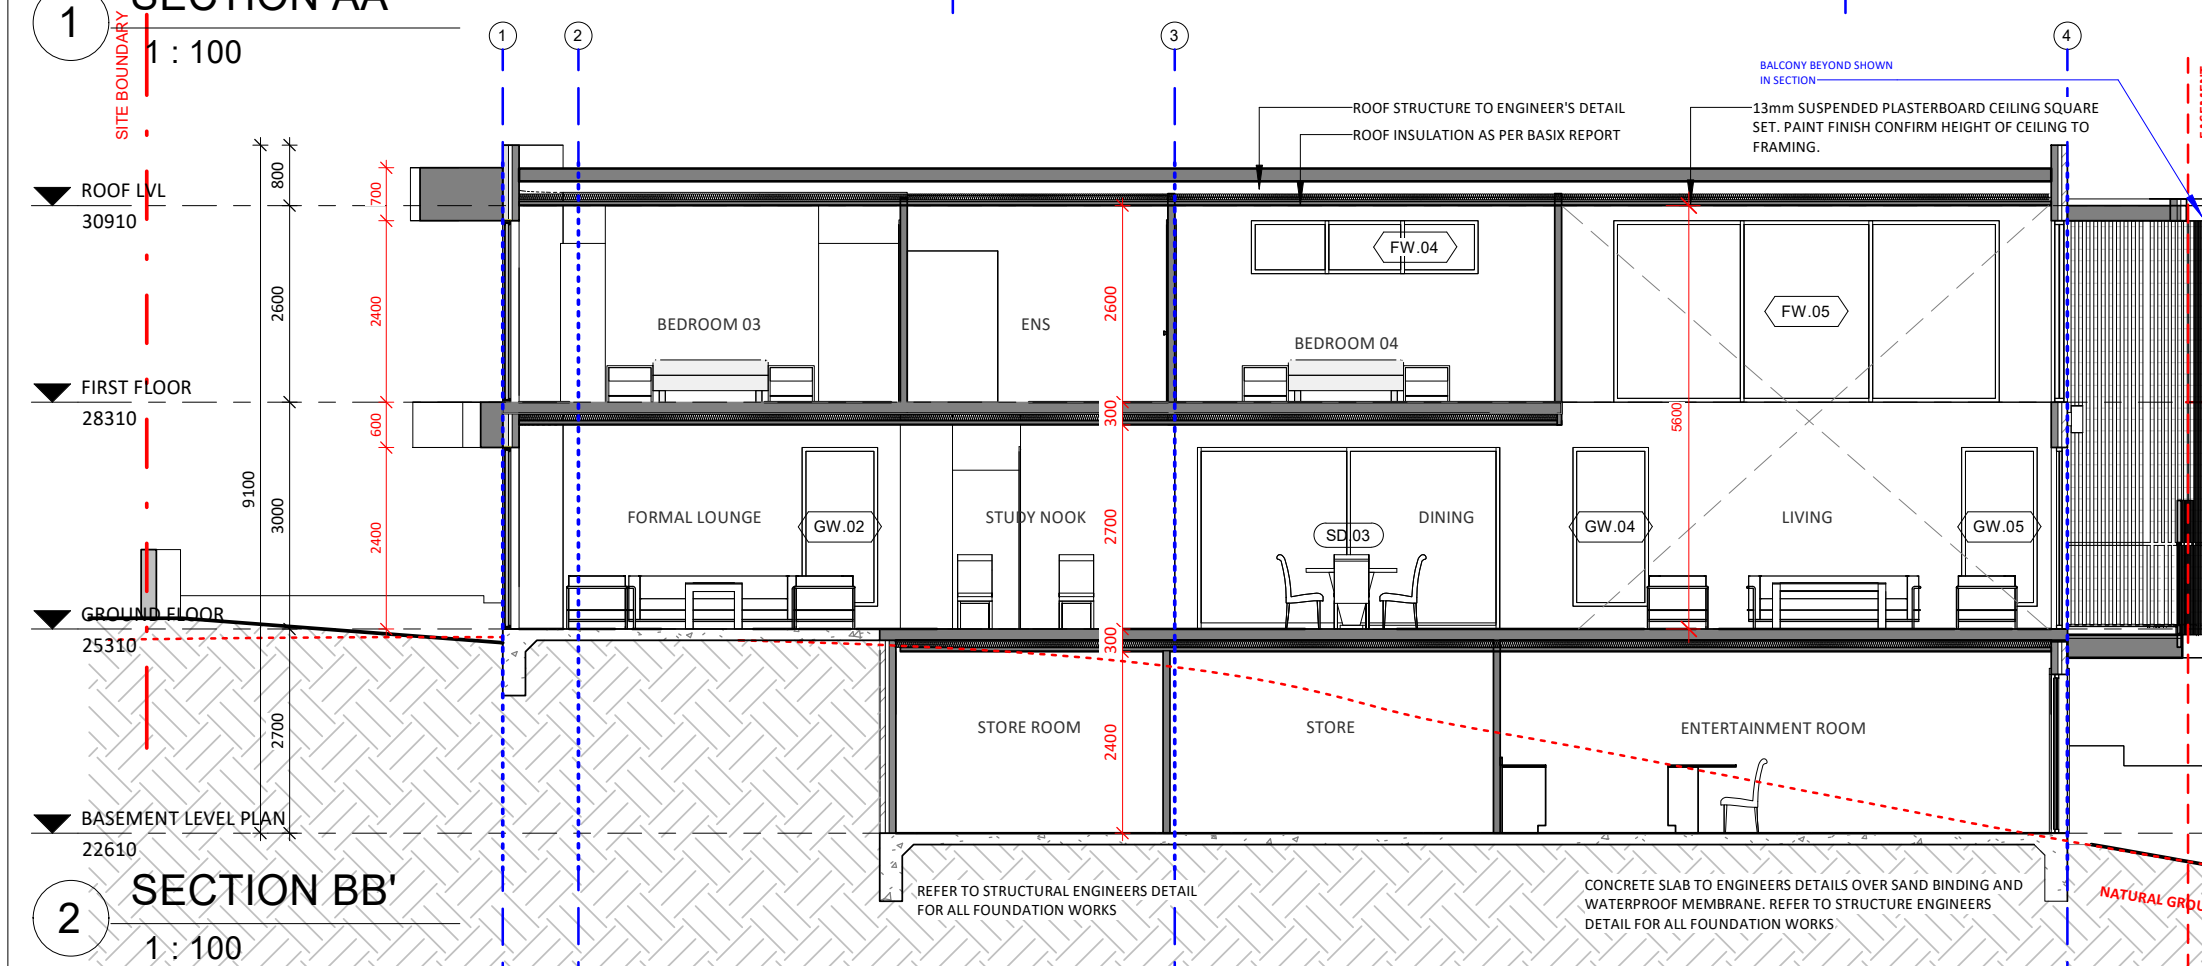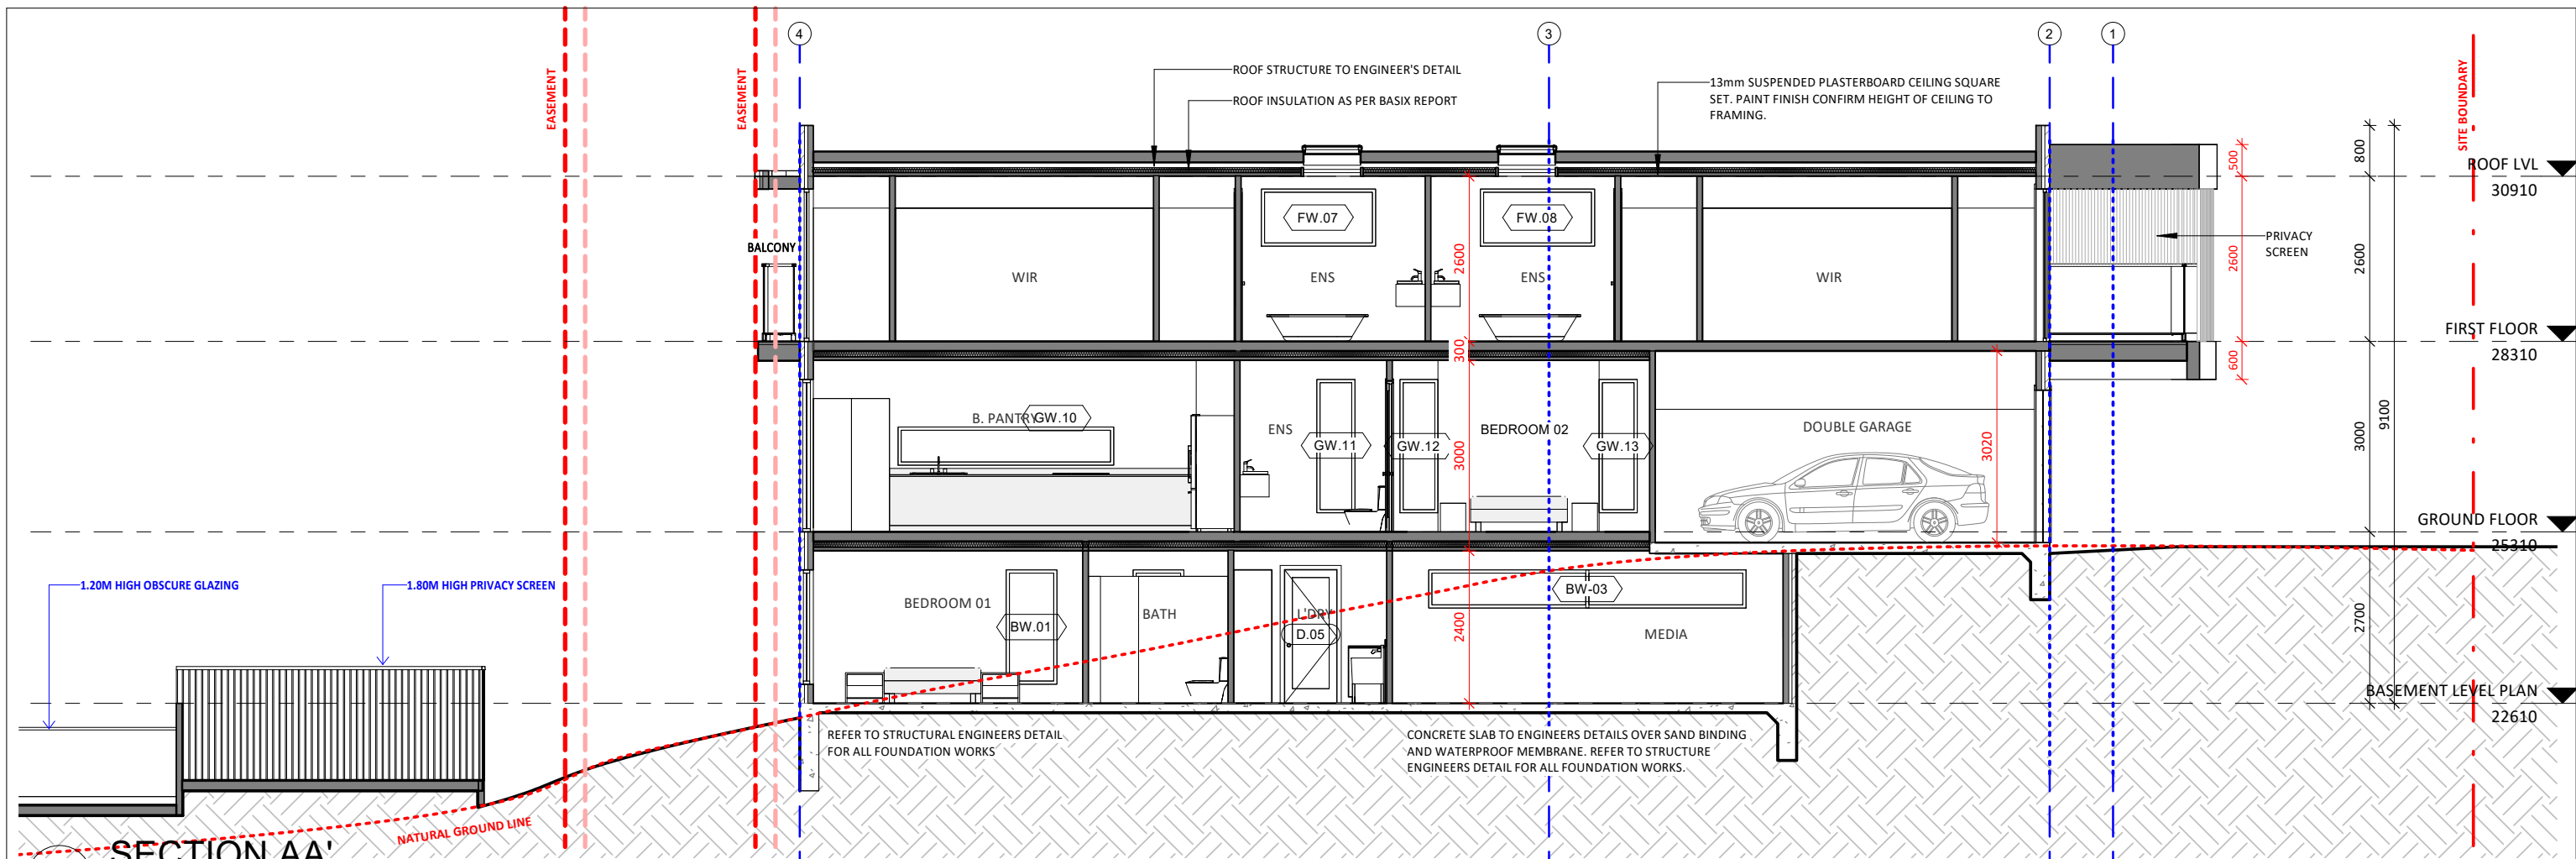

| REV. | DESCRIPTION                    | BY. | DATE       |
|------|--------------------------------|-----|------------|
| 1    | CONSTRUCTION CERTIFICATE ISSUE | AA  | 01/07/2025 |
| 2    | CONSTRUCTION CERTIFICATE       | AA  | 25/11/2025 |
|      |                                |     |            |
|      |                                |     |            |
|      |                                |     |            |

**NOTES**


- THESE DRAWINGS ARE PRELIMINARY DRAWINGS AND ARE SUBJECT TO CHANGE WITHOUT NOTICE DURING THE COURSE OF THE PROPOSED DEVELOPMENT AND IN CONSULTATION WITH COUNCIL.
- DRAWINGS MADE TO A LARGER SCALE AND THOSE SHOWING PARTICULAR DETAIL OF WORKS SHALL TAKE PRECEDENCE OVER DRAWINGS MADE TO A SMALLER SCALE AND FOR MORE GENERAL PURPOSES.
- WHERE ANY DISCREPANCY EXISTS BETWEEN FIGURED AND SCALED DIMENSIONS, THE FIGURED DIMENSIONS SHALL PREVAIL.
- BUILDER TO CHECK ALL SITE DIMENSIONS PRIOR TO FABRICATION OF FITMENTS.
- BEFORE CARRYING OUT ANY WORK ENSURE THAT THE DRAWINGS USED CARRY THE LATEST AMENDMENT NO.

THESE DOCUMENTS AND ANY WORKS EXECUTED AS A RESULT OF THESE DOCUMENTS SHALL BE SUBJECT TO THE COPYRIGHT CONDITIONS SET OUT IN THE CONDITIONS OF ENGAGEMENT ©


CLIENT  
ARCHITECT  
**STUDIOHAUS**  
E:CONNECT@STUDIOHAUS.COM.AU  
P:61433571784

| DRAWING TITLE  |                               | PROPOSED SECTIONS |      |
|----------------|-------------------------------|-------------------|------|
| PROJECT NUMBER | 156                           | DWG NUMBER        | A400 |
| SCALE          | 1:100                         | REVISION          | 2    |
| PROJECT        | LOT 515                       |                   |      |
| ADDRESS        | LOT 515, THORPE WAY, BOX HILL |                   |      |



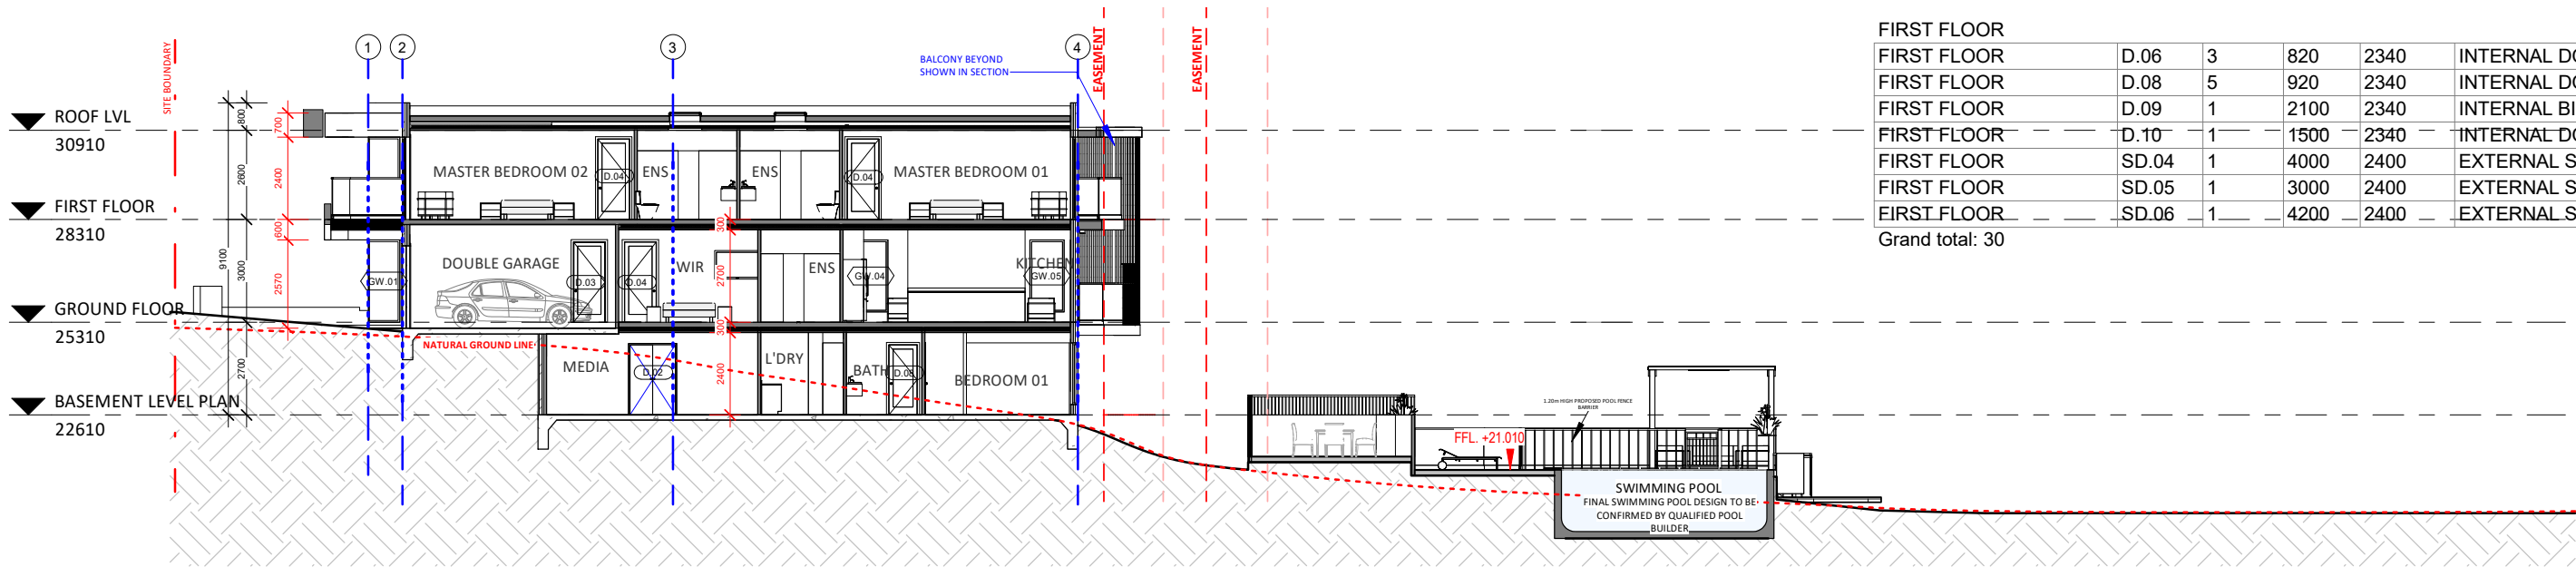

1 SITE SECTION CC'  
1 : 200

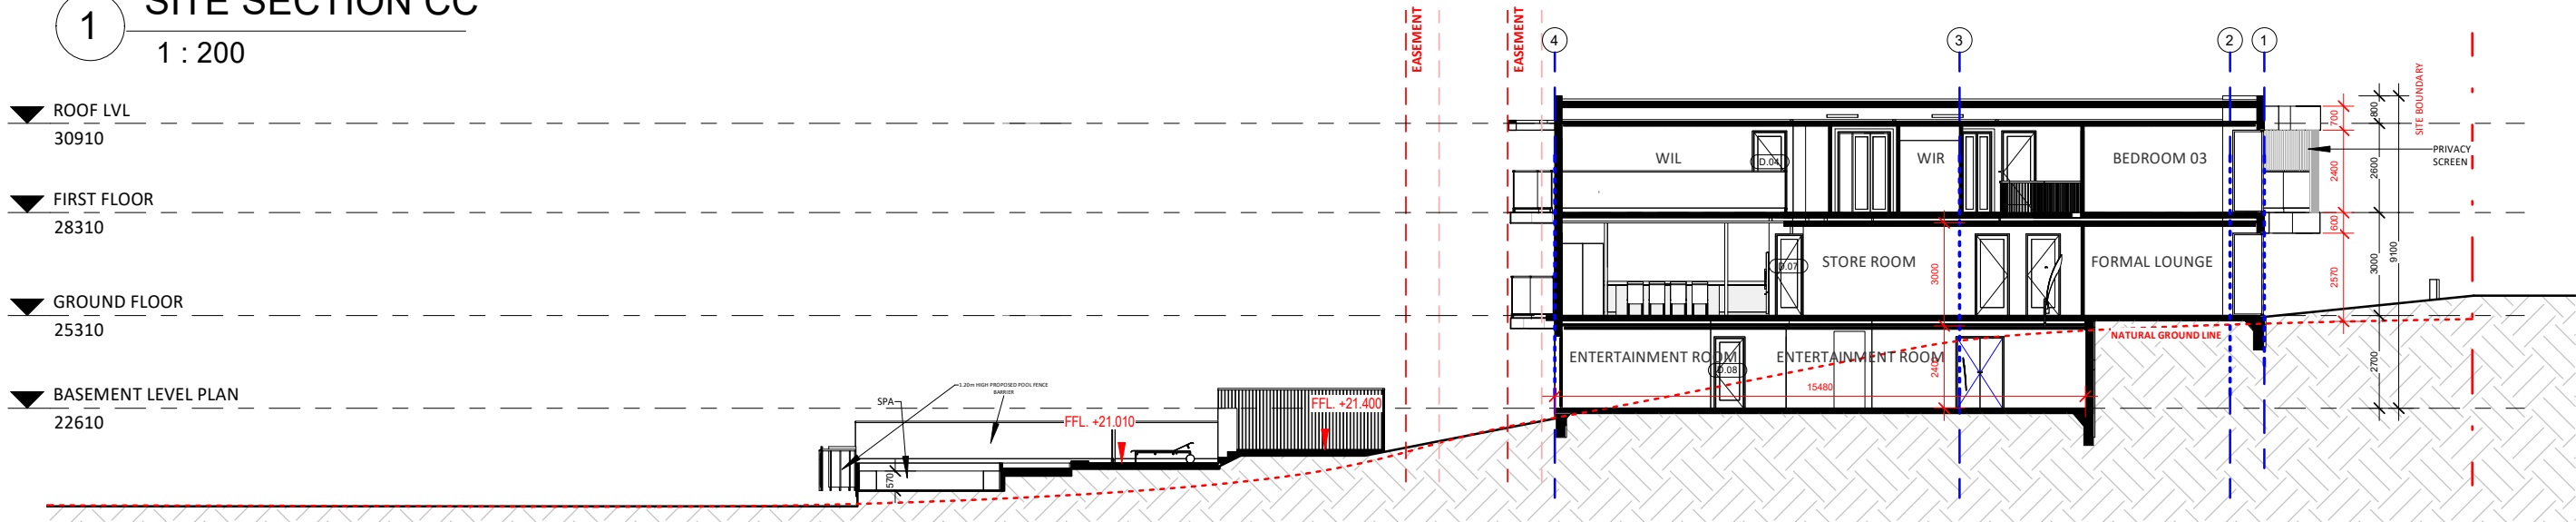

2 SITE SECTION DD'  
1 : 200

| REV. | DESCRIPTION                    | BY. | DATE       |
|------|--------------------------------|-----|------------|
| 1    | CONSTRUCTION CERTIFICATE ISSUE | AA  | 01/07/2025 |
| 2    | CONSTRUCTION CERTIFICATE       | AA  | 25/11/2025 |
|      |                                |     |            |
|      |                                |     |            |
|      |                                |     |            |

| NOTES   |
|---|
| -THESE DRAWINGS ARE PRELIMINARY DRAWINGS AND ARE SUBJECT TO CHANGE WITHOUT NOTICE DURING THE COURSE OF THE PROPOSED DEVELOPMENT AND IN CONSULTATION WITH COUNCIL.        |
| -DRAWINGS MADE TO A LARGER SCALE AND THOSE SHOWING PARTICULAR DETAIL OF WORKS SHALL TAKE PRECEDENCE OVER DRAWINGS MADE TO A SMALLER SCALE AND FOR MORE GENERAL PURPOSES. |
| -WHERE ANY DISCREPANCY EXISTS BETWEEN FIGURED AND SCALED DIMENSIONS, THE FIGURED DIMENSIONS SHALL PREVAIL.                                                               |
| -BUILDER TO CHECK ALL SITE DIMENSIONS PRIOR TO FABRICATION OF FITMENTS.                                                                                                  |
| -BEFORE CARRYING OUT ANY WORK ENSURE THAT THE DRAWINGS USED CARRY THE LATEST AMENDMENT NO.                                                                               |
| THESE DOCUMENTS AND ANY WORKS EXECUTED AS A RESULT OF THESE DOCUMENTS SHALL BE SUBJECT TO THE COPYRIGHT CONDITIONS SET OUT IN THE CONDITIONS OF ENGAGEMENT ©             |

| CLIENT                      |
|-----------------------------|
| ARCHITECT                   |
| STUDIOHAUS                  |
| E:CONNECT@STUDIOHAUS.COM.AU |
| P: +61433571784             |


| DRAWING TITLE                         | PROPOSED SITE SECTIONS |
|---------------------------------------|------------------------|
| PROJECT NUMBER 156                    | DWG NUMBER A401        |
| SCALE 1:200                           | REVISION 2 NORTH       |
| PROJECT LOT 515                       |                        |
| ADDRESS LOT 515, THORPE WAY, BOX HILL |                        |

| DOOR SCHEDULE       |       |       |       |        |               |
|---------------------|-------|-------|-------|--------|---------------|
| LEVEL               | MARK  | COUNT | WIDTH | HEIGHT | COMMENTS      |
| BASEMENT LEVEL PLAN |       |       |       |        |               |
| BASEMENT LEVEL PLAN | D.02  | 3     | 820   | 2040   | INTERNAL DOOR |
| BASEMENT LEVEL PLAN | D.03  | 1     | 1320  | 2040   | INTERNAL DOOR |
| BASEMENT LEVEL PLAN | D.04  | 2     | 920   | 2040   | INTERNAL DOOR |
| BASEMENT LEVEL PLAN | D.05  | 1     | 820   | 2100   | EXTERNAL DOOR |
| BASEMENT LEVEL PLAN | SD.01 | 1     | 4000  | 2100   | EXTERNAL DOOR |


|              |       |   |      |      |                       |
|--------------|-------|---|------|------|-----------------------|
| GROUND FLOOR |       |   |      |      |                       |
| GROUND FLOOR | D.01  | 1 | 2100 | 2400 | ENTRY DOOR            |
| GROUND FLOOR | D.06  | 2 | 820  | 2340 | INTERNAL DOOR         |
| GROUND FLOOR | D.07  | 1 | 720  | 2340 | INTERNAL DOOR         |
| GROUND FLOOR | D.08  | 2 | 920  | 2340 | INTERNAL DOOR         |
| GROUND FLOOR | GD    | 1 | 5000 | 2400 | GARAGE DOOR           |
| GROUND FLOOR | SD.02 | 1 | 6000 | 2400 | EXTERNAL SLIDING DOOR |
| GROUND FLOOR | SD.03 | 1 | 5000 | 2400 | EXTERNAL SLIDING DOOR |

|                 |       |   |      |      |                       |
|-----------------|-------|---|------|------|-----------------------|
| FIRST FLOOR     |       |   |      |      |                       |
| FIRST FLOOR     | D.06  | 3 | 820  | 2340 | INTERNAL DOOR         |
| FIRST FLOOR     | D.08  | 5 | 920  | 2340 | INTERNAL DOOR         |
| FIRST FLOOR     | D.09  | 1 | 2100 | 2340 | INTERNAL BI-FOLD DOOR |
| FIRST FLOOR     | D.10  | 1 | 1500 | 2340 | INTERNAL DOOR         |
| FIRST FLOOR     | SD.04 | 1 | 4000 | 2400 | EXTERNAL SLIDING DOOR |
| FIRST FLOOR     | SD.05 | 1 | 3000 | 2400 | EXTERNAL SLIDING DOOR |
| FIRST FLOOR     | SD.06 | 1 | 4200 | 2400 | EXTERNAL SLIDING DOOR |
| Grand total: 30 |       |   |      |      |                       |

Rendered Wall - Lexicon Qtr  
(RP1) (dulux or similar)

 

Window Frame - Monument  
(W) (dulux or similar)

 

Metal Roof- Basalt  
(MR) (colorbond or similar)



Balustrade- Glass  
(BAL) (viridian or similar)



Garage Door- Timber Look  
(GD) (colorbond or similar)



Conceptual View

| REV. | DESCRIPTION                    | BY. | DATE       | NOTES   | <div>CLIENT</div> <div>ARCHITECT</div> <div><div>STUDIOHAUS</div></div> <div>E:CONNECT@STUDIOHAUS.COM.AU</div> <div>P: +61433571784</div> | DRAWING TITLE  |                               | MATERIAL SCHEDULE |      |       |
|------|--------------------------------|-----|------------|---|---|----------------|-------------------------------|-------------------|------|-------|
| 1    | CONSTRUCTION CERTIFICATE ISSUE | AA  | 01/07/2025 | -THESE DRAWINGS ARE PRELIMINARY DRAWINGS AND ARE SUBJECT TO CHANGE WITHOUT NOTICE DURING THE COURSE OF THE PROPOSED DEVELOPMENT AND IN CONSULTATION WITH COUNCIL.<br>-DRAWINGS MADE TO A LARGER SCALE AND THOSE SHOWING PARTICULAR DETAIL OF WORKS SHALL TAKE PRECEDENCE OVER DRAWINGS MADE TO A SMALLER SCALE AND FOR MORE GENERAL PURPOSES<br>-WHERE ANY DISCREPANCY EXISTS BETWEEN FIGURED AND SCALED DIMENSIONS, THE FIGURED DIMENSIONS SHALL PREVAIL.<br>-BUILDER TO CHECK ALL SITE DIMENSIONS PRIOR TO FABRICATION OF FITMENTS<br>-BEFORE CARRYING OUT ANY WORK ENSURE THAT THE DRAWINGS USED CARRY THE LATEST AMENDMENT NO. |   | PROJECT NUMBER | 156                           | DWG NUMBER        | A700 |       |
| 2    | CONSTRUCTION CERTIFICATE       | AA  | 25/11/2025 |   |   | SCALE          |                               | REVISION          | 2    | NORTH |
|      |                                |     |            |   |   | PROJECT        | LOT 515                       |                   |      |       |
|      |                                |     |            |   |   | ADDRESS        | LOT 515, THORPE WAY, BOX HILL |                   |      |       |
|      |                                |     |            | THESE DOCUMENTS AND ANY WORKS EXECUTED AS A RESULT OF THESE DOCUMENTS SHALL BE SUBJECT TO THE COPYRIGHT CONDITIONS SET OUT IN THE CONDITIONS OF ENGAGEMENT ©   |   |                |                               |                   |      |       |